



ශ්‍රී ලංකා ප්‍රජාතාන්ත්‍රික සමාජවාදී ජනරජයේ ගැසට් පත්‍රය

අති විශේෂ

අංක 2469/29 – 2026 ජනවාරි මස 01 වැනි බ්‍රහස්පතින්දා – 2026.01.01

(රජයේ බලයපිට ප්‍රසිද්ධ කරන ලදී)

IV (අ) වැනි කොටස – පළාත් පාලනය

පළාත් පාලන නිවේදන

අයගම ප්‍රාදේශීය සභාව

1987 අංක 15 දරන ප්‍රාදේශීය සභා පනතේ 24 වන වගන්තිය සමග කියවිය යුතු, සබරගමුව පළාතේ ගරු ආණ්ඩුකාරතුමා විසින් අංක 2316/20 සහ 2023 ජනවාරි මස 24 වැනි දිනැති අති විශේෂ ගැසට් පත්‍රයේ ප්‍රකාශයට පත්කරනු ලැබ ඇති “සබරගමුව පළාතේ ප්‍රාදේශීය සභා විසින් පවත්වාගෙන යනු ලබන පාරවල් හා පටු මාවත්වල සැලසුම් පිළියෙල කිරීම හා නාම ලේඛනය දක්වමින් දැන්වීම් පළ කිරීම පිළිබඳ නියෝග ” මාලාවෙන් සබරගමුව පළාතේ ප්‍රාදේශීය සභාවලට පවරා දී ඇති කාර්යය අනුව , මෙහි පහත උපලේඛනයේ ඇතුළත් පාරවල් සහ පටු මාවත් අයගම ප්‍රාදේශීය සභාව සතු වී ඇති පාරවල් සහ පටු මාවත් වශයෙන් ප්‍රකාශයට පත් කළ යුතු බව 2025.12.11 දින පවත්වනු ලැබූ මහා සභා රැස්වීමේ අංක (06) 01 .36 - II යටතේ තීරණය කරනු ලැබ ඇති බව මහජනතාවගේ දැන ගැනීම සඳහා මෙයින් ප්‍රසිද්ධ කරනු ලැබේ.

එකී උපලේඛනයේ ඇතුළත් යම් පාරක් හෝ පටු මාවතක් කිසියම් ඉඩමක් හරහා හෝ යම් ඉඩමක කොටසකට ඇතුළත් වන බව , ඒ ඉඩමට හිමිකම් කියනු ලබන පාර්ශවයේ මතය වේ නම් , එකී ඉඩමට තමන්ගේ ඇති අයිතිය ඔප්පු කිරීම සඳහා මෙම නිවේදනයේ දින සිට මාස තුනක කාලයක් ඉකුත්වීමට පෙර නිසි අධිකරණයේ නඩුවක් පැවරීමට ක්‍රියා කළ යුතු බවත් මෙයින් නිවේදනය කරනු ලැබේ.

තව දුරටත් එසේම, එකී මාස තුනක කාලය අවසන් වීමට පෙර එවැනි නඩුවක් පවරා නැති එකී උපලේඛනයේ ඇතුළත් සෑම පාරක්ම සහ පටු මාවතක්ම අයගම ප්‍රාදේශීය සභාව සතු කරනු ලැබ ඇති පාරක් හෝ පටු මාවතක් ලෙස සලකනු ලබන බව වැඩිදුරටත් නිවේදනය කරනු ලැබේ.

ඒ.එම්.සී.කේ.සෙනෙවිරත්න,
ලේකම්,
අයගම ප්‍රාදේශීය සභාව.

2025 දෙසැම්බර් මස 30 වැනි දින,
අයගම ප්‍රාදේශීය සභාව,
අයගම දී ය.

අයගම ප්‍රාදේශීය සභාව

අයගම කලවාන ප්‍රධාන මාර්ගයට සම්බන්ධිත අයගම ප්‍රාදේශීය සභාවට අයත් මාර්ග නාමලේඛනය

අනු. අංකය	පාරෙහි කේතය	පාරේ නම	ආරම්භක බණ්ඩාංක (කදවල ශ්‍රී ලංකා)		අවසාන බණ්ඩාංක (කදවල ශ්‍රී ලංකා)		පාරේ දිග (මීටර්)	පාරේ සාමාන්‍ය පළල (මීටර්)	සංවර්ධිත පළල (මීටර්)
			වම	දකුණ	වම	දකුණ			
1	SG/ APS/ B034/ 01	පැළලීමෝදරවත්ත මාර්ගය	159876.947/ 148983.413	159874.112/ 148984.555	159905.907/ 149885.744	159906.975/ 149882.939	1352.2	3.0	2.5
2	SG/ APS/ B034/ 01/ 01	පැළලීමෝදරවත්ත ගම්සභා මාර්ගය	159877.497/ 149042.944	159878.751/ 149049.381	160030.782/ 149513.286	160027.886/ 149512.507	602.81	3.0	2.5
3	SG/ APS/ B034/ 02	අයගම අක්කර 08 යකඟවුවෙල මාර්ගය	159776.853/ 149052.16	159779.998/ 149049.682	160468.738/ 147891.991	160465.818/ 147894.809	1857.5	4.0	3.0
4	SG/ APS/ B034/ 02/ 01	මහපෝරුවකන්ද මාර්ගය	159735.011/ 149000.084	159735.439/ 148996.823	159373.122/ 148527.286	159375.522/ 148525.486	784.49	3.0	2.0
5	SG/ APS/ B034/ 02/ 02	වැරණියකැටිය මාර්ගය	159881.887/ 148705.505	159880.342/ 148701.478	159569.287/ 148483.953	159571.939/ 148486.947	529.65	4.0	2.5
6	SG/ APS/ B034/ 02/ 02/ 01	වැරණියකැටිය මාර්ගයේ පළමු පටුම	159700.651/ 148621.953	159697.668/ 148622.287	159689.727/ 148674.064	159686.763/ 148674.528	58.83	3.0	2.8
7	SG/ APS/ B034/ 02/ 02/ 02	වැරණියකැටිය මාර්ගයේ දෙවන පටුම	159676.864/ 148629.875	159670.766/ 148631.369	159648.827/ 148658.334	159645.965/ 148659.235	46.61	3.0	3.0

අනු. අංකය	පාලනික කේතය	පාලන නම	ආරම්භක බණ්ඩාංක (කදවල ශ්‍රී ලංකා)		අවසාන බණ්ඩාංක (කදවල ශ්‍රී ලංකා)		පාලන දිග (මීටර්)	පාලන සාමාන්‍ය පළල (මීටර්)	සංවර්ධන පළල (මීටර්)
			වම	දකුණ	වම	දකුණ			
8	SG/ APS/ B034/ 02/ 03	අක්කර 08 මාර්ගය	159896.163/ 148288.035	159893.565/ 148284.896	159044.8/ 148734.409	159043.773/ 148730.109	993.24	4.0	3.5
9	SG/ APS/ B034/ 02/ 04	වත්තලනකන්ද පහළ මාර්ගය	159879.35/ 148221.045	159877.375/ 148218.784	159479.305/ 148252.167	159476.739/ 148250.614	422.79	3.0	2.7
10	SG/ APS/ B034/ 02/ 05	අක්කර 08 වත්තලනකන්ද මාර්ගය	159863.257/ 148197.441	159863.872/ 148193.483	159857.93/ 147900.482	159859.376/ 147904.212	435.75	4.0	3.0
11	SG/ APS/ B034/ 02/ 05/ 01	අක්කර 08 වත්තලනකන්ද මාර්ගයේ පළමු පටුම	159717.39/ 148002.043	159718.897/ 147999.446	159572.467/ 147803.659	159574.459/ 147799.764	258.78	3.0	2.0
12	SG/ APS/ B034/ 02/ 06	කිතුල්ගල ඕකන්ද මාර්ගය	159927.749/ 148107.283	159930.172/ 148103.793	159871.823/ 148055.912	159875.25/ 148053.849	79.09	4.0	3.0
13	SG/ APS/ B034/ 02/ 06/ 01	කිතුල්ගල ඕකන්ද මාර්ගයේ පළමු පටුම	159872.751/ 148055.319	159874.309/ 148054.416	159846.304/ 148065.139	159845.591/ 148063.488	48.08	1.8	1.8
14	SG/ APS/ B034/ 02/ 07	වත්තලනකන්ද මාර්ගය	160406.523/ 147812.894	160410.882/ 147813.516	159301.816/ 147931.145	159305.283/ 147929.148	1514.7	4.0	3.5
15	SG/ APS/ B034/ 02/ 07/ 01	කැකුණගහණේ මාර්ගය	160409.473/ 147806.227	160410.098/ 147810.406	160319.044/ 147126.992	160322.993/ 147126.359	1036.9	4.0	3.5

අනු. අංකය	පාරමිති නිකේතය	පාරමිති නම	ආරම්භක බණ්ඩංක (කළුපිටි ලංකා)		අවසාන බණ්ඩංක (කළුපිටි ලංකා)		පාරමිති දිග (මීටර්)	පාරමිති පළල (මීටර්)	සංවර්ධන පළල (මීටර්)
			වම	දකුණ	වම	දකුණ			
16	SG/ APS/ B034/ 02/ 07/ 02	සුනිමලාරාමය මාර්ගය	160275.603/ 147707.697	160279.735/ 147709.571	160452.02/ 147575.579	160454.159/ 147578.349	228.15	3.5	2.6
17	SG/ APS/ B034/ 02/ 07/ 03	වත්තඉන්නකන්ද මාර්ගයේ පළමු	160123.442/ 147596.918	160124.761/ 147599.693	160270.834/ 147498.315	160271.575/ 147501.222	192.95	3.0	3.0
18	SG/ APS/ B034/ 02/ 07/ 04	මල්වෙල අතුරු අඩි පාර	160115.296/ 147583.669	160117.421/ 147586.06	160080.563/ 147501.059	160083.058/ 147499.39	116.49	3.0	2.0
19	SG/ APS/ B034/ 02/ 07/ 05	වත්තඉන්නකන්ද කැකුණගහණේ මාර්ගය	160029.201/ 147534.248	160032.641/ 147535.317	160417.467/ 147281.162	160415.341/ 147284.577	520.85	3.5	3.0
20	SG/ APS/ B034/ 03	පශු වෛද්‍ය නිලධාරී කාර්යාල මාර්ගය	159683.217/ 149143.266	159678.225/ 149151.754	159574.286/ 149243.05	159578.091/ 149243.562	217.39	4.0	3.0
21	SG/ APS/ B034/ 04	නිහතමානිගම සමරුගම තොරණගොඩ මාර්ගය	159499.955/ 149200.61	159496.052/ 149199.269	159377.076/ 149566.606	159379.326/ 149570.003	1401.7	4.0	3.5
22	SG/ APS/ B034/ 04/ 01	සරත්පුරය පළමු පවුම	159471.165/ 149219.603	159466.88/ 149220.591	159469.014/ 149295.972	159465.021/ 149295.734	72.66	4.0	3.0
23	SG/ APS/ B034/ 04/ 02	සරත්පුරය දෙවන පවුම	159392.077/ 149223.459	159390.157/ 149224.139	159356.266/ 149288.908	159352.841/ 149289.672	128.52	2.0	1.0

අනු. අංකය	පාරමිති නිකේතය	පාරමිති නම	ආරම්භක බණ්ඩාංක (කදවල ශ්‍රී ලංකා)		අවසාන බණ්ඩාංක (කදවල ශ්‍රී ලංකා)		පාරම් දිග (මීටර්)	පාරම් සාමාන්‍ය පළල (මීටර්)	සංවර්ධිත පළල (මීටර්)
			වම	දකුණ	වම	දකුණ			
24	SG/ APS/ B034/ 04/ 03	කොරවුවෙත්ත මාර්ගය	159250.253/ 149314.197	159256.987/ 149315.207	159249.113/ 149289.054	159251.528/ 149289.703	40.35	2.5	2.0
25	SG/ APS/ B034/ 04/ 04	සරත්පුරය සිට සුසානභූමිය දක්වා මාර්ගය	159117.957/ 149522.031	159116.825/ 149524.857	159275.288/ 149566.638	159273.2/ 149568.792	187.03	3.0	3.0
26	SG/ APS/ B034/ 04/ 05	නිහනමානිගම පහළ වක්‍ර මාර්ගය	159058.681/ 149552.921	159061.605/ 149551.934	159020.189/ 149590.958	159018.534/ 149593.463	460.36	3.0	3.0
27	SG/ APS/ B034/ 04/ 06	නිහනමානිගම බේරලියන මාර්ගය	158983.715/ 149677.2	158982.347/ 149673.256	158383.276/ 149913.921	158381.918/ 149910.023	833.08	4.0	3.5
28	SG/ APS/ B034/ 04/ 06/ 01	මහභේන වත්ත මාර්ගය	158964.351/ 149692.745	158961.299/ 149694.296	158998.977/ 150099.954	158996.351/ 150101.403	544.1	3.0	3.0
29	SG/ APS/ B034/ 04/ 07	සමරුගම සුසානභූමි මාර්ගය	159222.068/ 149663.818	159222.56/ 149662.789	159167.768/ 149577.524	159169.575/ 149577.603	109.07	1.0	1.0
30	SG/ APS/ B034/ 05	අක්කර 17 මාර්ගය	159211.519/ 149034.985	159218.216/ 149030.927	159041.303/ 148733.53	159047.967/ 148731.88	414.34	4.0	3.0
31	SG/ APS/ B034/ 05/ 01	අක්කර 17 මාර්ගයේ පළමු පටුම	159130.998/ 148885.536	159127.121/ 148884.22	159083.254/ 148926.653	159080.254/ 148924.85	66.63	3.5	3.0

අනු. අංකය	පාරෙහි නේතය	පාරේ නම	ආරම්භක බණ්ඩාංක (කළුපිලි ලංකා)		අවසාන බණ්ඩාංක (කළුපිලි ලංකා)		පාරේ දිග (මීටර්)	පාරේ සාමාන්‍ය පළල (මීටර්)	සංවර්ධිත පළල (මීටර්)
			වම	දකුණ	වම	දකුණ			
32	SG/ APS/ B034/ 05/ 02	අක්කර 17 උඩුවික්කන්ද මාර්ගය	159044.8/ 148734.409	159043.773/ 148730.109	158125.354/ 149478.274	158121.421/ 149477.302	1973.6	4.0	3.0
33	SG/ APS/ B034/ 05/ 02/ 01	අක්කර 17 උඩුවික්කන්ද මාර්ගයේ පළමු පටුම	159021.748/ 148734.947	159025.062/ 148734.705	158796.759/ 148656.29	158795.047/ 148653.825	470.44	3.0	2.0
34	SG/ APS/ B034/ 05/ 02/ 01/ 01	අක්කර 17 උඩුවික්කන්ද මාර්ගයේ පළමු පටුමගෙහි පළමු අතුරු මාර්ගය	158991.422/ 148548.772	158992.385/ 148549.052	159057.796/ 148519.906	159058.97/ 148519.778	84.02	1.0	1.0
35	SG/ APS/ B034/ 05/ 02/ 02	අක්කර 17 බලිගල තලපත්ගල මාර්ගය	158790.021/ 148650.333	158794.837/ 148653.525	158382.198/ 147780.059	158385.922/ 147778.599	1370.6	4.0	3.0
36	SG/ APS/ B034/ 05/ 02/ 02/ 01	අක්කර 17 බලිගල තලපත්ගල මාර්ගයේ පළමු පටුම	158817.423/ 148519.898	158817.439/ 148528.493	158838.804/ 148127.09	158822.184/ 148132.745	639.36	4.0	3.0
37	SG/ APS/ B034/ 05/ 02/ 03	අක්කර 17 උඩුවික්කන්ද මාර්ගයේ දෙවන පටුම	158438.414/ 148763.884	158435.909/ 148765.709	158503.197/ 148862.357	158500.647/ 148860.779	128.87	3.0	3.0
38	SG/ APS/ B034/ 06	ඇරපෝරුව පළමු මාර්ගය	158948.58/ 149198.35	158950.482/ 149197.656	158925.977/ 149044.689	158927.188/ 149046.282	175.85	2.0	2.0
39	SG/ APS/ B034/ 07	භංගුල්ල ඇරපෝරුව මාර්ගය	158756.919/ 149280.358	158751.859/ 149280.624	158853.235/ 149666.474	158851.455/ 149670.328	493.5	4.0	3.0

අනු-අංකය	පාරෙහි නේතය	පාරේ නම	ආරම්භක බණ්ඩාංක (කදවල ශ්‍රී ලංකා)		අවසාන බණ්ඩාංක (කදවල ශ්‍රී ලංකා)		පාරේ දිග (මීටර්)	පාරේ සාමාන්‍ය පළල (මීටර්)	සංවර්ධිත පළල (මීටර්)
			වම	දකුණ	වම	දකුණ			
40	SG/ APS/ B034/ 08	බතලවත්ත මාර්ගය	158734.228/ 149276.134	158737.683/ 149275.567	159079.02/ 148828.925	159080.342/ 148832.184	641.26	3.5	3.0
41	SG/ APS/ B034/ 09	බෙරලියන නැගිරිකන්ද මාර්ගය	158343.692/ 149536.821	158333.851/ 149536.613	157532.409/ 151660.94	157528.419/ 151661.227	3195	4.0	3.0
42	SG/ APS/ B034/ 09/ 01	බෙරලියන නැගිරිකන්ද මාර්ගයේ පළමු පටුම	158588.658/ 150216.398	158590.104/ 150219.052	158692.325/ 150185.096	158693.417/ 150187.89	1110.23	3.0	2.0
43	SG/ APS/ B034/ 09/ 02	බෙරලියන නැගිරිකන්ද මාර්ගයේ දෙවන පටුම	158627.329/ 150277.199	158626.656/ 150280.344	158689.683/ 150433.452	158692.408/ 150432.198	351.56	3.0	3.0
44	SG/ APS/ B034/ 09/ 03	බෙරලියන නැගිරිකන්ද මාර්ගයේ තෙවන පටුම	158111.976/ 150987.353	158112.465/ 150991.438	158275.157/ 151205.948	158271.209/ 151206.585	306.03	4.0	3.0
45	SG/ APS/ B034/ 09/ 03/ 01	බෙරලියන නැගිරිකන්ද මාර්ගයේ තෙවන පටුමගෙහි පළමු අතුරු මාර්ගය	158154.744/ 150992.508	158156.61/ 150997.015	158299.236/ 150956.415	158301.233/ 150959.881	161.88	4.0	3.0
46	SG/ APS/ B034/ 09/ 04	බෙරලියන නැගිරිකන්ද මාර්ගයේ සිව්වන පටුම	157834.276/ 151232.737	157836.717/ 151228.902	157712.493/ 151213.456	157714.3/ 151209.888	141.11	4.0	4.0
47	SG/ APS/ B034/ 09/ 05	බෙරලියන නැගිරිකන්ද මාර්ගයේ පස්වන පටුම	157738.073/ 151409.432	157739.279/ 151405.489	157651.773/ 151359.443	157651.821/ 151355.433	103.89	4.0	4.0
48	SG/ APS/ B034/ 09/ 06	බෙරලියන නැගිරිකන්ද මාර්ගයේ පස්වන පටුම	157740.857/ 151414.172	157738.739/ 151412.038	157645.585/ 151601.7	157643.157/ 151603.606	236.88	3.0	3.0

අනු. අංකය	පාරෙහි කෝනය	පාරේ නම	ආරම්භක බණ්ඩංක (කළුපිලි ලංකා)		අවසාන බණ්ඩංක (කළුපිලි ලංකා)		පාරේ දිග (මීටර්)	පාරේ සාමාන්‍ය පළල (මීටර්)	සංවර්ධිත පළල (මීටර්)
			වම	දකුණ	වම	දකුණ			
49	SG/ APS/ B034/ 10	මදනගොඩ සිට උඩුගල දක්වා මාර්ගය	158181.837/ 149530.177	158184.494/ 149528.738	157391.423/ 149936.971	157396.102/ 149933.757	1022.9	3.0	3.0
50	SG/ APS/ B034/ 10/ 01	මදනගොඩ සිට උඩුගල දක්වා මාර්ගයේ පළමු පටුම	158011.146/ 149532.548	158013.627/ 149532.226	158005.128/ 149421.695	158007.541/ 149422.344	137.14	2.5	2.5
51	SG/ APS/ B034/ 10/ 02	පරගල ඕවිට පළමු පටු මාර්ගය	157873.215/ 149556.686	157875.354/ 149554.572	157702.551/ 149441.812	157700.574/ 149439.557	230.08	3.0	3.0
52	SG/ APS/ B034/ 10/ 02/ 01	පරගල ඕවිට පළමු පටු මාර්ගයේ අතුරු මාර්ගය	157863.022/ 149546.611	157866.47/ 149548.22	157875.338/ 149462.628	157875.905/ 149465.575	94.72	3.0	3.0
53	SG/ APS/ B034/ 10/ 03	පරගල ඕවිට දෙවන පටු මාර්ගය	157834.076/ 149624.615	157835.474/ 149621.555	157643.499/ 149637.885	157644.625/ 149635.105	203.97	3.0	3.0
54	SG/ APS/ B034/ 10/ 04	මදනගොඩ සිට උඩුගල දක්වා මාර්ගයේ දෙවන පටුම	157572.746/ 149848.72	157574.867/ 149848.169	157407.661/ 149823.444	157411.3/ 149823.103	209.54	2.0	2.0
55	SG/ APS/ B034/ 11	සිරිවර්ධනවත්ත පළමු මාර්ගය	158119.974/ 149611.359	158117.772/ 149613.678	158097.966/ 150266.167	158097.965/ 150269.167	797	3.0	3.0
56	SG/ APS/ B034/ 11/ 01	සිරිවර්ධනවත්ත පළමු මාර්ගයේ පළමු පටුම	158165.277/ 149982.886	158164.765/ 149979.875	158001.442/ 150157.23	158000.977/ 150154.266	278.05	3.0	3.0

අනු. අංකය	පාරෙහි කේතය	පාරේ නම	ආරම්භක බණ්ඩංක (කළවල ශ්‍රී ලංකා)		අවසාන බණ්ඩංක (කළවල ශ්‍රී ලංකා)		පාරේ දිග (මීටර්)	පාරේ සාමාන්‍ය පළල (මීටර්)	සංවර්ධිත පළල (මීටර්)
			වම	දකුණ	වම	දකුණ			
67	SG/ APS/ B034/ 17/ 03	උඩුගල නවජනපදය මාර්ගයේ තෙවන පටුම	157179.764/ 150851.724	157183.032/ 150849.121	157144.654/ 150802.344	157146.314/ 150798.704	64.78	4.0	3.0
68	SG/ APS/ B034/ 17/ 04	උඩුගල නවජනපදය මාර්ගයේ ඔබ්බෙන් පටුම	157200.963/ 150891.536	157203.824/ 150894.019	157287.029/ 150857.015	157287.488/ 150859.98	97.11	3.0	3.0
69	SG/ APS/ B034/ 17/ 05	උඩුගල නවජනපදය මාර්ගයේ පස්වන පටුම	157216.086/ 150916.647	157213.762/ 150913.39	157127.214/ 150981.919	157125.388/ 150978.36	123.59	4.0	3.0
70	SG/ APS/ B034/ 18	අක්කර 20 මාර්ගය	156877.268/ 150804.353	156877.963/ 150800.9	156656.696/ 150684.219	156654.526/ 150679.967	304.82	3.5	3.0
71	SG/ APS/ B034/ 19	පරගල මේ කර්මාන්තශාලා මාර්ගය	156572.965/ 151531.534	156566.092/ 151530.921	156786.029/ 151735.844	156782.224/ 151737.077	510.48	4.0	3.5
72	SG/ APS/ B034/ 20	මානකන්ද දවලකැටිය පරගලවත්ත මාර්ගය	156360.177/ 151676.944	156359.953/ 151672.728	155883.786/ 151411.51	155887.773/ 151411.84	611.81	4.0	2.6
73	SG/ APS/ B034/ 20/ 01	පරගල කෝඩ්ගෙදුවත්ත මාර්ගය	156168.376/ 151640.022	156171.544/ 151642.503	156236.059/ 151404.622	156238.258/ 151401.282	358.16	4.0	2.5
74	SG/ APS/ B034/ 20/ 02	පරගල මානකන්ද මාර්ගය	156169.797/ 151646.132	156166.453/ 151643.627	155789.695/ 151426.375	155792.419/ 151429.304	593.3	4.0	2.5
75	SG/ APS/ B034/ 20/ 02/ 01	පරගල කෙසෙල්කොටුව මාර්ගය	156157.289/ 151679.199	156154.634/ 151682.46	156034.065/ 151783.759	156034.102/ 151780.759	207.91	3.0	2.0

අනු. අංකය	පාරමිති කේතය	පාරමිති නම	ආරම්භක බණ්ඩාංක (කදවල ශ්‍රී ලංකා)		අවසාන බණ්ඩාංක (කදවල ශ්‍රී ලංකා)		පාරම් දිග (මීටර්)	පාරමිති පළල (මීටර්)	සංවර්ධිත පළල (මීටර්)
			වම	දකුණ	වම	දකුණ			
76	SG/ APS/ B034/ 20/ 02/ 02	පරගල මානකන්ද මාර්ගයේ පළමු පටුම	156010.801/ 151671.013	156007.863/ 151670.303	155883.58/ 151868.857	155881.899/ 151871.343	342.96	3.0	2.4
77	SG/ APS/ B034/ 20/ 02/ 03	පරගලකන්ද මාර්ගය	155843.954/ 151581.64	155840.732/ 151579.269	155314.994/ 151842.066	155311.916/ 151839.512	638.21	4.0	2.5
78	SG/ APS/ B034/ 20/ 02/ 04	මානකන්ද පරගලකන්ද මාර්ගය	155772.657/ 151521.694	155771.718/ 151517.214	155589.382/ 151354.958	155591.602/ 151352.94	284.75	3.0	1.0
79	SG/ APS/ B034/ 21	පරගල ගලට්ටකන්ද නිවැසිල්ල මාර්ගය	156373.909/ 151711.103	156373.201/ 151716.646	156792.033/ 153926.13	156788.576/ 153926.675	2579.91	3.5	3.0
80	SG/ APS/ B034/ 21/ 01	කොඩිකාරපංගුව මාර්ගය	156538.424/ 151964.35	156536.76/ 151960.071	156381.863/ 151983.084	156385.862/ 151982.999	214.84	4.0	2.5
81	SG/ APS/ B034/ 21/ 02	කිවිලිමහ නොඩිකාරපංගුව මාර්ගය	156546.391/ 152043.263	156548.149/ 152048.114	156787.385/ 151893.95	156791.09/ 151895.46	310.94	4.0	3.0
82	SG/ APS/ B034/ 21/ 02/ 01	කිවිලිමහ නොඩිකාරපංගුව මාර්ගයේ පළමු පටුම	156598.289/ 152032.348	156594.757/ 152034.194	156898.787/ 152008.165	156898.007/ 152011.062	321.58	3.0	2.0
83	SG/ APS/ B034/ 21/ 03	ගලට්ටකන්ද පළමු පටුම	156571.617/ 152309.337	156570.741/ 152312.83	156623.027/ 152278.37	156626.563/ 152277.695	83.32	3.6	3.0
84	SG/ APS/ B034/ 21/ 04	ගලට්ටකන්ද බතලවත්ත මාර්ගය	156573.555/ 152773.207	156574.564/ 152768.959	156404.175/ 152802.831	156402.073/ 152799.428	188.43	4.0	3.5

අනු. අංකය	පාරෙහි නෝනය	පාරේ නම	ආරම්භක බණ්ඩාංක (කළුපිටි ලිංකා)		අවසාන බණ්ඩාංක (කළුපිටි ලිංකා)		පාරේ දිග (මීටර්)	පාරේ සාමාන්‍ය පළල (මීටර්)	සංවර්ධිත පළල (මීටර්)
			වම	දකුණ	වම	දකුණ			
85	SG/ APS/ B034/ 21/ 05	පරගල ගලට්ටිකන්ද නිරිඳුල්ල අරඹ අඩි පාර	156607.192/ 152840.292	156608.18/ 152843.295	156645.905/ 152795.527	156648.802/ 152796.306	65.93	3.0	2.5
86	SG/ APS/ B034/ 22	පරගල අමුණේකන්ද මාර්ගය	156311.263/ 151852.193	156308.847/ 151853.986	156339.724/ 151947.712	156337.826/ 151949.633	114.43	2.7	2.5
87	SG/ APS/ B034/ 23	පරගල අමුණේකන්ද මාර්ගය	156018.482/ 152154.787	156015.62/ 152153.686	156165.389/ 152193.153	156167.56/ 152195.224	280.02	3.0	2.5
88	SG/ APS/ B034/ 24	පරගල පොකුණුදොළ මාර්ගය	155906.959/ 152234.496	155903.953/ 152235.52	156005.52/ 152398.007	156004.741/ 152400.905	221.13	3.0	2.5
89	SG/ APS/ B034/ 25	පරගල කිරිමැටිහේන මාර්ගය	155605.488/ 152254.823	155610.423/ 152254.601	155213.861/ 151898.401	155212.207/ 151895.898	756	3.0	2.6
90	SG/ APS/ B034/ 26	මීනමල්වත්ත ගලට්ටිකන්ද මාර්ගය	155548.83/ 152342.896	155544.417/ 152344.581	156481.018/ 152489.773	156485.08/ 152492.253	1680	4.0	3.0
91	SG/ APS/ B034/ 26/ 01	ගෙවත්තහේන මාර්ගය පළමු පටුමග	155812.259/ 152854.083	155807.217/ 152852.988	155881.989/ 152886.323	155882.927/ 152890.212	90.69	4.0	3.0
92	SG/ APS/ B034/ 26/ 02	ගෙවත්තහේන මාර්ගය දෙවන පටුමග	156137.361/ 152707.502	156135.173/ 152709.799	156172.151/ 152815.675	156169.384/ 152814.517	151.73	3.0	3.0
93	SG/ APS/ B034/ 26/ 03	ගෙවත්තහේන මාර්ගය තෙවන පටුමග	156141.391/ 152699.11	156145.003/ 152698.151	156061.22/ 152612.179	156064.117/ 152612.958	148.28	3.0	2.5

අනු-අංකය	පාරමිති නම	ආරම්භක බණ්ඩාංක (කදවල ශ්‍රී ලංකා)		අවසාන බණ්ඩාංක (කදවල ශ්‍රී ලංකා)		පාරේ දිග (මීටර්)	පාරේ සාමාන්‍ය පළල (මීටර්)	සංවර්ධිත පළල (මීටර්)
		වම	දකුණ	වම	දකුණ			
94	SG/ APS/ B034/ 27	155206.007/ 152563.527	155204.082/ 152567.05	155242.19/ 152686.466	155238.344/ 152687.568	154.24	4.0	3.5
95	SG/ APS/ B034/ 28	154869.536/ 152691.801	154873.824/ 152690.24	154751.073/ 152596.152	154754.425/ 152598.333	221.14	4.0	3.5
96	SG/ APS/ B034/ 29	154809.16/ 152802.307	154805.185/ 152807.601	154907.573/ 152813.606	154908.043/ 152817.578	124.81	4.0	2.0
97	SG/ APS/ B034/ 30	154427.166/ 153082.404	154420.883/ 153083.167	155488.137/ 152921.174	155487.906/ 152925.667	1275.64	4.5	4.0
98	SG/ APS/ B034/ 30/ 01	154792.381/ 153158.865	154787.287/ 153159.596	154753.1/ 153504.337	154749.634/ 153506.333	415.23	4.0	3.5
99	SG/ APS/ B034/ 30/ 01/ 01	154742.638/ 153222.09	154745.056/ 153218.001	154408.76/ 153347.892	154408.756/ 153343.891	374.39	4.0	3.5
100	SG/ APS/ B034/ 30/ 02	154998.718/ 153197	154993.134/ 153197.319	155037.456/ 153256.341	155035.567/ 153259.866	77.55	4.0	3.5
101	SG/ APS/ B034/ 30/ 03	155179.961/ 153156.997	155176.157/ 153158.242	155353.978/ 153314.694	155349.98/ 153314.623	304.23	4.0	3.5

අනු. අංකය	පාරමිති කේතය	පාරමිති නම	ආරම්භක බණ්ඩංක (කළුපිටි ලිංකා)		අවසාන බණ්ඩංක (කළුපිටි ලිංකා)		පාරමිති දිග (මීටර්)	පාරමිති සාමාන්‍ය පළල (මීටර්)	සංවර්ධන පළල (මීටර්)
			වම	දකුණ	වම	දකුණ			
102	SG/ APS/ B034/ 31	පිල්ලවත්ත මාර්ගය	154406.068/ 153077.414	154411.176/ 153077.68	154202.873/ 152646.25	154203.992/ 152642.41	520.81	4.0	3.0
103	SG/ APS/ B034/ 31/ 01	වැලිකොටුපොළ මාර්ගය	154338.58/ 152979.364	154338.638/ 152974.272	154245.307/ 153028.339	154245.823/ 153024.372	114.48	4.0	3.0
104	SG/ APS/ B034/ 31/ 02	පිල්ලවත්ත මාර්ගයේ පළමු පටුම	154350.511/ 152910.575	154352.063/ 152913.891	154496.07/ 152867.97	154498.125/ 152870.803	166.47	3.5	3.0
105	SG/ APS/ B034/ 31/ 03	පිල්ලවත්ත මාර්ගය	154304.71/ 152834.973	154305.897/ 152837.782	154522.292/ 152705.741	154521.95/ 152708.722	364.55	3.0	2.5
106	SG/ APS/ B034/ 31/ 03/ 01	පිල්ලවත්ත මාර්ගය	154388.387/ 152674.926	154392.563/ 152675.194	154550.972/ 152553.484	154548.342/ 152555.792	236.12	3.5	2.5
107	SG/ APS/ B034/ 31/ 04	පිල්ලවත්ත සිට ගෝණපැනිගල මාර්ගය	154275.162/ 152791.666	154274.09/ 152788.334	154205.965/ 152809.811	154206.026/ 152806.312	73.42	3.5	3.0
108	SG/ APS/ B034/ 32	පිඬුර ඉහළවත්ත අඩි පාර	154012.825/ 153424.749	154009.586/ 153424.804	154003.812/ 153644.448	154001.169/ 153645.868	246.52	3.0	2.0

අනු. අංකය	පාරමිති කේතය	පාරමිති නම	ආරම්භක බණ්ඩාංක (කදවල ශ්‍රී ලංකා)		අවසාන බණ්ඩාංක (කදවල ශ්‍රී ලංකා)		පාරමිති දිග (මීටර්)	පාරමිති පළල (මීටර්)	සංවර්ධිත පළල (මීටර්)
			වම	දකුණ	වම	දකුණ			
109	SG/ APS/ B034/ 33	අම්බලන්වෙල මාර්ගය	153461.878/ 153590.973	153458.194/ 153589.411	153411.402/ 153660.025	153410.345/ 153656.167	116.18	4.0	3.5
110	SG/ APS/ B034/ 34	ගෝඨභූමිගල මාර්ගය	153396.573/ 153201.848	153398.804/ 153204.009	154081.918/ 152867.054	154082.727/ 152869.943	817.68	3.0	2.5
111	SG/ APS/ B034/ 35	භේනියාය මාර්ගයේ පළමු කොටස	153389.272/ 152995.541	153393.184/ 152998.685	153341.616/ 152602.786	153341.848/ 152598.292	482.11	4.5	4.0
112	SG/ APS/ B034/ 35/ 01	මානකන්ද මාර්ගය	153430.222/ 152736.929	153435.079/ 152739.957	154342.32/ 152408.172	154342.144/ 152412.168	1190.1	4.0	3.5
113	SG/ APS/ B034/ 35/ 01/ 01	මානකන්ද මාර්ගයේ පළමු පටුම	153899.665/ 152576.357	153895.645/ 152579.514	153984.239/ 152618.235	153981.568/ 152620.496	101.89	3.5	3.0
114	SG/ APS/ B034/ 35/ 01/ 02	මානකන්ද මාර්ගයේ දෙවන පටුම	154039.118/ 152485.79	154036.953/ 152488.545	154106.259/ 152595.084	154104.673/ 152598.204	134.09	3.5	3.0
115	SG/ APS/ B034/ 35/ 01/ 03	මානකන්ද මාර්ගයේ තෙවන පටුම	154041.481/ 152462.55	154041.738/ 152459.016	153662.298/ 152526.853	153659.966/ 152524.243	405.75	3.5	3.0
116	SG/ APS/ B034/ 35/ 01/ 04	මානකන්ද මාර්ගයේ සිව්වන පටුම	154126.013/ 152332.949	154130.983/ 152333.176	154153.784/ 152303.817	154154.445/ 152307.255	48.53	3.5	3.0
117	SG/ APS/ B034/ 35/ 02	කුඹුරුගේ මාර්ගය	153368.378/ 152619.278	153372.246/ 152625.574	153339.415/ 151563.978	153342.627/ 151565.367	1204.47	3.5	3.0

අනු. අංකය	පාරෙහි නේතය	පාරේ නම	ආරම්භක බණ්ඩංක (කළමනාකරණ ලංකා)		අවසාන බණ්ඩංක (කළමනාකරණ ලංකා)		පාරේ දිග (මීටර්)	පාරේ සාමාන්‍ය පළල (මීටර්)	සංවර්ධිත පළල (මීටර්)
			වම	දකුණ	වම	දකුණ			
118	SG/ APS/ B034/ 36	කිවිලිගේ මාර්ගය	153305.628/ 153129.141	153306.867/ 153125.338	153206.548/ 152910.147	153210.448/ 152911.03	285.42	4.0	3.0
119	SG/ APS/ B034/ 37	කදවැල්ලේ මාර්ගය	153249.311/ 153215.57	153252.33/ 153213.785	152981.28/ 152948.11	152983.391/ 152943.015	423.1	3.5	3.0
120	SG/ APS/ B034/ 38	හතේ කණුව සිට කදවැල්ලේ මාර්ගය	153053.703/ 153278.299	153056.199/ 153276.109	152948.854/ 152799.077	152951.034/ 152796.734	1122	3.2	3.0
121	SG/ APS/ B034/ 38/ 01	වැවුණ්ගේ මාර්ගය	152713.194/ 153309.444	152711.435/ 153304.691	152375.237/ 153406.448	152373.893/ 153403.216	366.85	3.5	3.0
122	SG/ APS/ B034/ 38/ 02	ටකරන්වත්ත මාර්ගය	152680.037/ 153166.182	152682.453/ 153163.284	152597.369/ 153144.862	152598.195/ 153141.461	94.28	3.5	3.0
123	SG/ APS/ B034/ 39	අල්ලකොඩි සිට පිඹුර මාර්ගය	153159.174/ 153546.815	153157.519/ 153553.13	153482.772/ 153802.755	153479.861/ 153807.714	613.27	4.0	3.6
124	SG/ APS/ B034/ 40	අලුත්ගෙවත්ත මාර්ගය	153010.665/ 153748.025	153009.109/ 153751.891	153219.447/ 153770.356	153216.519/ 153773.082	268.12	4.0	4.0
125	SG/ APS/ B034/ 41	එගොඩවත්ත මාර්ගය	152952.76/ 153792.175	152954.849/ 153789.182	152590.784/ 154044.446	152595.397/ 154047.95	764.66	3.5	3.0
126	SG/ APS/ B034/ 42	එපිටවත්ත මාර්ගය	152873.971/ 153877.869	152877.218/ 153875.483	152835.639/ 153831.498	152838.333/ 153828.542	65.1	4.0	3.7

අනු-අංකය	පාරෙහි නම	පාරේ නම	ආරම්භක බණ්ඩාංක (කදවල ශ්‍රී ලංකා)		අවසාන බණ්ඩාංක (කදවල ශ්‍රී ලංකා)		පාරේ දිග (මීටර්)	පාරේ සාමාන්‍ය පළල (මීටර්)	සංවර්ධිත පළල (මීටර්)
			වම	දකුණ	වම	දකුණ			
127	SG/ APS/ B034/ 43	නිකගොඩ උඩවත්ත මාර්ගය	152657.431/ 154083.67	152654.879/ 154083.362	152360.208/ 154587.182	152360.132/ 154584.673	713.87	2.5	2.0
128	SG/ APS/ B034/ 44	නිකගොඩ උඩකුඹුර පළමු මාර්ගය	152348.275/ 154207.188	152352.569/ 154205.401	152199.322/ 154093.296	152202.807/ 154092.968	227.71	3.5	2.8
129	SG/ APS/ B034/ 45	නිකගොඩ අළුතේ මාර්ගය	152293.939/ 154277.524	152292.666/ 154282.208	151888.105/ 155763.132	151885.466/ 155765.432	1893.83	3.5	3.0
130	SG/ APS/ B034/ 45/ 01	අළුතේ සුදුවැලිපොත මාර්ගය	152356.698/ 154587.11	152356.43/ 154583.337	152159.211/ 154687.009	152157.809/ 154683.802	265.83	3.5	3.0
131	SG/ APS/ B034/ 45/ 02	නිකගොඩ අළුතේ මාර්ගයේ පළමු පටුම	151857.452/ 155248.606	151858.086/ 155245.608	151465.03/ 155520.798	151466.274/ 155518.069	539.24	3.0	3.0
132	SG/ APS/ B034/ 45/ 03	නිකගොඩ අළුතේ මාර්ගයේ දෙවන පටුම	151863.251/ 155311.934	151863.102/ 155316.035	152001.775/ 155288.691	152004.081/ 155291.959	155.73	4.0	3.5
133	SG/ APS/ B034/ 45/ 04	නිකගොඩ අළුතේ මාර්ගයේ තෙවන පටුම	151801.975/ 155463.935	151800.363/ 155460.522	151732.14/ 155523.606	151729.672/ 155521.122	101.62	3.5	3.0
134	SG/ APS/ B034/ 45/ 05	නිකගොඩ අළුතේ මාර්ගයේ සිව්වන පටුම	151836.428/ 155524.305	151834.142/ 155521.646	151834.407/ 155586.377	151835.461/ 155589.714	117.35	3.5	3.0

අනු. අංකය	පාරෙහි නේතය	පාරේ නම	ආරම්භක බණ්ඩංගු (කළුපිට ලිංකා)		අවසාන බණ්ඩංගු (කළුපිට ලිංකා)		පාරේ දිග (මීටර්)	පාරේ සාමාන්‍ය පළල (මීටර්)	සංවර්ධිත පළල (මීටර්)
			වම	දකුණ	වම	දකුණ			
135	SG/ APS/ B034/ 46	නිකගොඩ උඩුකුඹුර දෙවන මාර්ගය	152258.501/ 154304.292	152263.252/ 154301.889	152204.333/ 154227.006	152207.714/ 154227.914	141.05	3.5	3.0
136	SG/ APS/ B034/ 47	නිකගොඩ උඩුකුඹුර තෙවන මාර්ගය	152069.276/ 154356.638	152072.633/ 154356.714	152142.219/ 154268.253	152144.721/ 154269.909	121.34	3.0	2.6
137	SG/ APS/ B034/ 48	නිකගොඩ පළමු පටුම	151954.285/ 154343.495	151957.929/ 154340.37	151929.476/ 154249.566	151930.281/ 154252.456	221.65	3.0	2.5
138	SG/ APS/ B034/ 49	අක්කර 08 ඇල්ලකඩේවත්ත මාර්ගය	151611.061/ 154472.237	151614.777/ 154471.403	151773.68/ 154023.63	151774.069/ 154020.655	760.82	3.0	3.0
139	SG/ APS/ B034/ 49/ 01	අක්කර 05 ඉඹුලභිටිහේන මාර්ගය	151938.098/ 154056.691	151941.446/ 154057.97	151932.947/ 153924.582	151934.081/ 153921.271	182.92	3.5	3.0
140	SG/ APS/ B034/ 50	නිකගොඩ ගොවිපොළ මාර්ගය	151211.374/ 154544.621	151203.484/ 154546.446	151235.423/ 154749.043	151236.685/ 154745.247	436.11	4.0	3.5
141	SG/ APS/ B034/ 51	හල්ගහහේන මාර්ගය	150926.637/ 154660.74	150923.79/ 154661.863	151152.756/ 154757.59	151154.921/ 154759.668	334.47	3.0	2.8
142	SG/ APS/ B034/ 52	හැඬබෑවහේන මාර්ගය	150683.495/ 154788.477	150679.725/ 154789.884	150827.894/ 155031.371	150830.496/ 155033.973	730.23	3.7	3.0
143	SG/ APS/ B034/ 52/ 01	හැඬබෑවහේන මාර්ගයේ පළමු පටුම	150621.161/ 155143.169	150617.249/ 155142.86	150647.233/ 155275.072	150643.57/ 155274.726	137.17	3.7	3.0
144	SG/ APS/ B034/ 52/ 02	හැඬබෑවහේන මාර්ගයේ දෙවන පටුම	150789.859/ 155060.569	150786.209/ 155063.43	150892.89/ 155196.562	150889.895/ 155198.701	193.95	3.7	3.0

අනු. අංකය	පාරමිති නිකේතය	පාරමිති	ආරම්භක බණ්ඩාංක (කදවල ශ්‍රී ලංකා)		අවසාන බණ්ඩාංක (කදවල ශ්‍රී ලංකා)		පාරමිති දිග (මීටර්)	පාරමිති පළල (මීටර්)	සංවර්ධන පළල (මීටර්)
			වම	දකුණ	වම	දකුණ			
145	SG/ APS/ B034/ 53	හේතියාය මාර්ගයේ දෙවන කොටස	150599.829/ 154744.569	150604.025/ 154746.216	151605.162/ 153221.781	151608.029/ 153225.251	2437.9	4.5	4.0
146	SG/ APS/ B034/ 53/ 01	හේතියාය මාර්ගයේ දෙවන කොටසේ පළමු පටුම	150901.005/ 154361.832	150897.724/ 154364.184	150941.086/ 154398.682	150937.589/ 154400.624	56.74	4.0	3.7
147	SG/ APS/ B034/ 53/ 02	හේතියාය මාර්ගයේ දෙවන කොටසේ දෙවන පටුම	150915.379/ 154325.617	150916.725/ 154321.271	150779.801/ 154122.92	150783.759/ 154123.499	277.12	4.0	3.5
148	SG/ APS/ B034/ 53/ 03	හේතියාය මාර්ගයේ දෙවන කොටසේ තෙවන පටුම	150956.967/ 154236.316	150955.374/ 154240.109	151083.371/ 154306.853	151079.378/ 154307.09	151.05	4.0	3.5
149	SG/ APS/ B034/ 53/ 04	පොල්වත්ත කලුලහේනියාය මාර්ගය	151280.724/ 153714.697	151277.754/ 153717.657	151723.026/ 153871.479	151724.304/ 153875.269	889.95	4.0	3.6
150	SG/ APS/ B034/ 53/ 05	පොල්වත්ත කොස්ගහහේන මාර්ගය	151285.14/ 153710.987	151281.635/ 153713.771	151446.688/ 153665.393	151450.429/ 153666.811	209.62	4.0	3.7
151	SG/ APS/ B034/ 53/ 06	පොල්ලවත්ත මිරිස්හේන මාර්ගය	151566.103/ 153465.149	151565.211/ 153468.661	152196.977/ 153652.594	152193.511/ 153653.566	760.52	3.6	3.2
152	SG/ APS/ B034/ 53/ 06/ 01	පොල්ලවත්ත මිරිස්හේන මාර්ගයේ පළමු පටුම	151726.981/ 153602.314	151729.907/ 153603.013	151852.779/ 153438.163	151852.292/ 153441.124	250.01	3.0	3.0
153	SG/ APS/ B034/ 53/ 06/ 02	පොල්ලවත්ත මිරිස්හේන මාර්ගයේ දෙවන පටුම	151938.141/ 153656.04	151942.147/ 153656.042	151937.134/ 153620.166	151939.911/ 153623.044	37.22	4.0	3.5

අනු. අංකය	පාරෙහි නේතය	පාරේ නම	ආරම්භක බණ්ඩංක (කළුපිලි ලංකා)		අවසාන බණ්ඩංක (කළුපිලි ලංකා)		පාරේ දිග (මීටර්)	පාරේ සාමාන්‍ය පළල (මීටර්)	සංවර්ධිත පළල (මීටර්)
			වම	දකුණ	වම	දකුණ			
154	SG/ APS/ B034/ 53/ 06/ 03	පොල්ලවත්ත මිරිස්මේන් මාර්ගයේ තෙවන පටුම	151953.98/ 153659.429	151958.172/ 153663.244	151999.971/ 153630.358	152002.072/ 153633.762	59.18	4.0	3.5
155	SG/ APS/ B034/ 53/ 06/ 04	පොල්ලවත්ත මිරිස්මේන් මාර්ගයේ සිව්වන පටුම	152047.02/ 153658.921	152043.299/ 153660.465	152055.735/ 153689.167	152052.301/ 153687.115	37.6	4.0	3.7
156	SG/ APS/ B034/ 53/ 07	පොල්ලවත්ත පන්සල මාර්ගය	151594.161/ 153234.354	151588.103/ 153236.539	151564.82/ 153306.85	151560.827/ 153306.625	112.84	4.0	3.5
157	SG/ APS/ B034/ C404/ 01	ඇල්ලඕව්ට මාර්ගය	160232.449/ 148423.492	160234.269/ 148419.848	160102.703/ 148258.795	160106.689/ 148259.126	274.56	4.0	3.5
158	SG/ APS/ B034/ C404/ 02	අයගම ප්‍රාදේශීය සභාව අසල මාර්ගය	160277.687/ 148300.551	160275.962/ 148303.6	160360.472/ 148318.25	160361.682/ 148321.535	100.54	3.5	2.5
159	SG/ APS/ B034/ C404/ 03	අයගම ගලේ පන්සල මාර්ගය	160514.894/ 147862.732	160512.387/ 147864.916	161099.332/ 148315.776	161100.116/ 148318.981	1238.5	3.3	3.3
160	SG/ APS/ B034/ C404/ 04	අයගම ගෝණපලවත්ත මාර්ගය	160664.062/ 147685.186	160661.14/ 147687.992	160692.86/ 147811.045	160690.171/ 147809.713	165.78	3.0	3.0

අනු-අංකය	පාරෙහි නේතය	පාරේ නම	ආරම්භක බණ්ඩාංක (කදවල ශ්‍රී ලංකා)		අවසාන බණ්ඩාංක (කදවල ශ්‍රී ලංකා)		පාරේ දිග (මීටර්)	පාරේ සාමාන්‍ය පළල (මීටර්)	සංවර්ධිත පළල (මීටර්)
			වම	දකුණ	වම	දකුණ			
161	SG/ APS/ B034/ C404/ 05	යකඟුවෙල පින්තූන් මාර්ගය	160703.313/ 147661.927	160707.299/ 147661.312	160874.516/ 146570.34	160876.68/ 146573.853	1755.1	4.0	3.5
162	SG/ APS/ B034/ C404/ 05/ 01	විටෝරි මාර්ගය	160882.102/ 146903.71	160881.546/ 146904.545	160919.215/ 146948.385	160918.248/ 146948.684	62.65	1.0	1.0
163	SG/ APS/ B034/ C404/ 05/ 02	යකඟුවෙල පින්තූන් ඒ කොටස මාර්ගයේ පළමු පටුම	160737.493/ 146781.269	160742.01/ 146768.491	160483.043/ 146788.777	160479.708/ 146786.569	313.38	4.0	3.5
164	SG/ APS/ B034/ C404/ 06	අමුණුඹවි මාර්ගය	161113.758/ 147357.258	161115.071/ 147355.093	160997.494/ 147284.759	160999.217/ 147282.947	172.08	2.5	2.0
165	SG/ APS/ B034/ C404/ 07	පල්ලෙකඩ ලියන්ගමත්ත මාර්ගය	161319.55/ 147244.647	161317.94/ 147247.179	161595.737/ 147295.555	161595.182/ 147298.504	334.92	3.0	3.0
166	SG/ APS/ B034/ C404/ 08	පල්ලෙකඩ කලටුවකන්ද මාර්ගය	161589.331/ 146890.54	161590.577/ 146893.912	163580.055/ 146010.311	163581.573/ 146013.464	2723	3.5	3.0
167	SG/ APS/ B034/ C404/ 08/ 01	පල්ලෙකඩ කලටුවකන්ද මාර්ගයේ පළමු පටුම	161765.24/ 146834.981	161762.385/ 146837.761	162260.645/ 146827.904	162261.944/ 146831.153	592.87	3.5	3.0
168	SG/ APS/ B034/ C404/ 08/ 01/ 01	පල්ලෙකඩ කලටුවකන්ද මාර්ගයේ පළමු පටුමගෙහි පළමු අතුරු මාර්ගය	161877.614/ 146942.89	161874.052/ 146943.326	161836.74/ 147058.352	161834.092/ 147056.064	130.08	3.5	3.0
169	SG/ APS/ B034/ C404/ 08/ 01/ 02	පල්ලෙකඩ කලටුවකන්ද මාර්ගයේ පළමු පටුමගෙහි දෙවන අතුරු මාර්ගය	162068.884/ 146903.431	162064.528/ 146903.699	162065.967/ 147192.316	162063.483/ 147189.851	363.6	3.5	3.0

අනු. අංකය	පාරෙහි නෝනය	පාරේ නම	ආරම්භක බණ්ඩංක (කළුපිටි ලංකා)		අවසාන බණ්ඩංක (කළුපිටි ලංකා)		පාරේ දිග (මීටර්)	පාරේ සාමාන්‍ය පළල (මීටර්)	සංවර්ධිත පළල (මීටර්)
			වම්	දකුණ	වම්	දකුණ			
170	SG/ APS/ B034/ C404/ 08/ 02	පල්ලකඩ කලවුකන්ද මාර්ගයේ දෙවන පටුම	162095.484/ 146610.42	162092.231/ 146612.057	162075.851/ 146720.112	162072.543/ 146718.972	159.95	3.5	3.0
171	SG/ APS/ B034/ C404/ 08/ 03	පල්ලකඩ කලවුකන්ද මාර්ගයේ තෙවන පටුම	162235.225/ 146567.227	162231.787/ 146568.616	162277.016/ 146608.193	162274.259/ 146609.377	67.91	3.0	2.5
172	SG/ APS/ B034/ C404/ 08/ 04	පල්ලකඩ කලවුකන්ද මාර්ගයේ සිව්වන පටුම	162330.51/ 146539.017	162327.516/ 146539.222	162327.146/ 146639.195	162324.43/ 146637.919	119.75	3.0	2.5
173	SG/ APS/ B034/ C404/ 08/ 05	පල්ලකඩ කලවුකන්ද මාර්ගයේ පස්වන පටුම	162878.678/ 146452.22	162879.894/ 146456.27	162965.425/ 146459.726	162966.543/ 146463.043	113.09	3.5	3.0
174	SG/ APS/ B034/ C404/ 08/ 06	පල්ලකඩ කලවුකන්ද මාර්ගයේ සයවන පටුම	163249.055/ 146310.42	163251.852/ 146306.72	163186.802/ 146249.491	163185.128/ 146245.858	101.44	4.0	3.5
175	SG/ APS/ B034/ C404/ 08/ 07	පල්ලකඩ කලවුකන්ද මාර්ගයේ හත්වන පටුම	163349.292/ 146179.163	163350.69/ 146182.28	163466.236/ 146261.559	163469.087/ 146263.589	210.97	3.5	3.0
176	SG/ APS/ B034/ C404/ 09	පල්ලකඩ විටෝට්ට මාර්ගය	161542.933/ 146841.653	161545.476/ 146844.786	160870.378/ 146980.519	160869.878/ 146976.55	762.46	4.0	3.0
177	SG/ APS/ B034/ C404/ 09/ 01	විටෝට්ට බට්ටල දේවාල මාර්ගය	161530.816/ 146859.802	161526.513/ 146860.001	161513.995/ 146908.75	161510.7/ 146906.482	54.77	4.0	3.0

අනු-අංකය	පාරෙහි නේතය	පාරේ නම	ආරම්භක බණ්ඩාංක (කදවල ශ්‍රී ලංකා)		අවසාන බණ්ඩාංක (කදවල ශ්‍රී ලංකා)		පාරේ දිග (මීටර්)	පාරේ සාමාන්‍ය පළල (මීටර්)	සංවර්ධිත පළල (මීටර්)
			වම	දකුණ	වම	දකුණ			
178	SG/ APS/ B034/ C404/ 09/ 02	පල්ලෙකඩ විටෝට්ට මාර්ගයේ පළමු පටුම	161244.901/ 146852.016	161247.853/ 146851.472	161170.512/ 146835.73	161171.291/ 146832.833	88.88	3.0	3.0
179	SG/ APS/ B034/ C404/ 10	පල්ලෙකඩ කපුගෙවත්ත පළමු මාර්ගය	161473.741/ 146680.398	161471.855/ 146677.447	161178.081/ 146730.885	161181.339/ 146729.607	331.29	3.5	3.0
180	SG/ APS/ B034/ C404/ 11	පල්ලෙකඩ කපුගෙවත්ත දෙවන මාර්ගය	161465.864/ 146666.822	161464.162/ 146663.758	161370.433/ 146707.203	161370.628/ 146703.708	112.86	3.5	3.0
181	SG/ APS/ B034/ C404/ 12	පල්ලෙකඩ කපුගෙවත්ත තෙවන මාර්ගය	161319.608/ 146495.3	161318.655/ 146491.334	161145.813/ 146562.262	161144.251/ 146558.58	192.67	4.0	3.5
182	SG/ APS/ B034/ C404/ 13	බෝගහවංගුව අතුරු මාර්ගය	160804.117/ 146384.218	160801.495/ 146382.584	160452.028/ 146512.394	160453.507/ 146509.784	418.81	3.0	3.0
183	SG/ APS/ B034/ C404/ 13/ 01	බෝගහවෙල පළමු පටුම	160714.613/ 146378.184	160717.357/ 146376.873	160680.716/ 146305.937	160683.448/ 146304.696	81.59	3.0	3.0
184	SG/ APS/ B034/ C404/ 13/ 02	බෝගහවෙල දෙවන පටුම	160663.341/ 146420.705	160665.793/ 146418.821	160614.46/ 146365.428	160615.045/ 146362.485	80.35	3.0	3.0
185	SG/ APS/ B034/ C404/ 14	පිටකන්ද ඕලුවිලකන්ද මාර්ගය	160597.821/ 145684.591	160599.598/ 145687.607	160793.718/ 145549.191	160795.465/ 145552.225	245.86	3.5	2.7
186	SG/ APS/ B034/ C404/ 15	පිටකන්ද මල්ගහනේ මාර්ගය	160800.708/ 145218.773	160803.44/ 145216.441	160467.232/ 143887.714	160470.507/ 143889.052	1695.5	3.5	2.5

අනු. අංකය	පාරම්පරික නිකේතය	පාරම්පරික නම	ආරම්භක බණ්ඩාංක (කළුපිටි ලිංකා)		අවසාන බණ්ඩාංක (කළුපිටි ලිංකා)		පාරම්පරික දිග (මීටර්)	පාරම්පරික පළල (මීටර්)	සංවර්ධන පළල (මීටර්)
			වම	දකුණ	වම	දකුණ			
187	SG/ APS/ B034/ C404/ 15/ 01	පිටකන්ද මල්ගහගේන පළමු පවුම	160667.954/ 144809.794	160667.565/ 144806.819	160250.128/ 145116.823	160248.197/ 145114.528	554.23	3.0	3.0
188	SG/ APS/ B034/ C404/ 16	ගවරගිරිය පළමු පවුම	161128.747/ 144589.87	161128.216/ 144586.652	161049.572/ 144682.218	161046.572/ 144682.209	147.67	3.0	3.0
189	SG/ APS/ B034/ C404/ 17	ගවරගිරිය දෙවන පවුම	161135.292/ 144579.446	161135.64/ 144582.433	161180.913/ 144512.54	161182.41/ 144515.14	130.99	3.0	3.0
190	SG/ APS/ B034/ C404/ 18	ගවරගිරිය තෙවන පවුම	161127.88/ 144464.7	161127.449/ 144461.227	161062.547/ 144493.465	161062.922/ 144489.985	77.67	3.5	3.0
191	SG/ APS/ B034/ C404/ 19	ගවරගිරිය රයිගමකන්ද දුම්රියමාර්ග මාර්ගය	161779.411/ 143034.835	161779.803/ 143040.087	164105/ 141682.101	164098.104/ 141693.573	2828	5.0	2.8
192	SG/ APS/ B034/ C404/ 19/ 01	රයිගමකන්ද පළමු පවුම	162472.51/ 142538.194	162477.055/ 142538.346	162926.879/ 142179.351	162924.239/ 142181.648	598.79	3.5	2.5
193	SG/ APS/ B034/ C404/ 20	චතුකාරගම පුවත්තේ මාර්ගය	161830.697/ 142377.098	161831.329/ 142372.877	161658.235/ 142284.563	161660.779/ 142281.477	200.13	4.0	2.5
194	SG/ APS/ B034/ C404/ 20/ 01	චතුකාරගම ගල්වත්ත මාර්ගය	161770.912/ 142351.185	161767.49/ 142348.967	161407.504/ 142626.852	161406.567/ 142622.963	484.68	4.0	2.5
195	SG/ APS/ B034/ C404/ 21	චතුකාරගම ඇගිහිකන්න මාර්ගය	161854.188/ 142336.153	161857.671/ 142334.179	162065.157/ 142085.338	162069.155/ 142085.488	465.95	4.0	2.5

අනු. අංකය	පාරමිති නිකේතය	පාරමිති නාම	ආරම්භක බණ්ඩාංක (කදවල ශ්‍රී ලංකා)		අවසාන බණ්ඩාංක (කදවල ශ්‍රී ලංකා)		පාරමිති දිග (මීටර්)	පාරමිති පළල (මීටර්)	සංවර්ධිත පළල (මීටර්)
			වම	දකුණ	වම	දකුණ			
196	SG/ APS/ B034/ C404/ 21/ 01	චතුකාරමගම ඇගිලිකනක්ක මාර්ගයේ පළමු පටුම	161853.994/ 142265.949	161857.565/ 142259.677	161772.003/ 142238.716	161770.111/ 142236.387	210.73	3.0	2.5
197	SG/ APS/ B034/ C404/ 22	චතුකාරමගම දොරලඳිය මාර්ගය	162332.269/ 142015.546	162336.192/ 142013.515	162224.993/ 141974.511	162227.987/ 141971.858	124.22	4.0	3.0
198	SG/ APS/ B034/ C404/ D405/ 01	පල්ලෙකඩ වැලිකඩවත්ත මාර්ගය	161844.513/ 146592.528	161847.643/ 146590.71	161750.31/ 146468.354	161753.01/ 146467.049	233.54	3.0	2.0
199	SG/ APS/ B034/ C404/ D405/ 02	පල්ලෙකඩ ගමිකන්ද පළමු පටුම	162037.316/ 146402.471	162040.726/ 146400.334	162174.399/ 145975.895	162175.937/ 145979.587	563.2	4.0	2.7
200	SG/ APS/ B034/ C404/ D405/ 03	පල්ලෙකඩ ගමිකන්ද දෙවන පටුම	162453.292/ 146174.872	162456.176/ 146173.464	162428.868/ 145826.889	162431.61/ 145825.195	399.09	3.0	2.5
201	SG/ APS/ B034/ C404/ D405/ 04	පල්ලෙකඩ කලටුවකන්ද පළමු පටුම	162474.041/ 146170.034	162470.718/ 146171.919	162504.53/ 146482.959	162500.934/ 146484.458	488.03	3.8	3.0
202	SG/ APS/ B034/ C404/ D405/ 05	පල්ලෙකඩ කලටුවකන්ද දෙවන පටුම අඩි පාර	162686.261/ 146095.816	162683.748/ 146096.055	162811.398/ 146422.064	162808.898/ 146422.148	478.88	2.5	1.0
203	SG/ APS/ B034/ C404/ D405/ 06	ගංගොඩකන්ද මැල්ගොඩැල්ල මාර්ගය	162968.06/ 145953.49	162965.454/ 145954.98	163006.478/ 146187.935	163003.508/ 146188.359	262.04	3.0	2.6
204	SG/ APS/ B034/ C404/ D405/ 07	ගංගොඩකන්ද අක්කර 60 කලටුවකන්ද මාර්ගය	163512.077/ 145858.981	163508.787/ 145861.253	163471.577/ 146000.074	163469.503/ 145995.972	176.79	3.0	2.0

අනු. අංකය	පාරෙහි නේතය	පාරේ නම	ආරම්භක බණ්ඩංග (කළුපිලි ලංකා)		අවසාන බණ්ඩංග (කළුපිලි ලංකා)		පාරේ දිග (මීටර්)	පාරේ සාමාන්‍ය පළල (මීටර්)	සංවර්ධිත පළල (මීටර්)
			වම	දකුණ	වම	දකුණ			
205	SG/ APS/ B034/ C404/ D405/ 08	වටකුරුගල මාර්ගය	163588.386/ 145811.609	163591.924/ 145808.958	164489.39/ 144732.269	164490.466/ 144736.122	1968.8	4.0	3.3
206	SG/ APS/ B034/ C404/ D405/ 08/ 01	වටකුරුගල හේන්යාය මාර්ගය	163566.841/ 145755.912	163568.726/ 145759.463	163965.736/ 145418.686	163968.755/ 145414.624	645.72	4.0	3.5
207	SG/ APS/ B034/ C404/ D405/ 08/ 02	ඇල්ලේව හේන්යාය මාර්ගය	163496.965/ 145572.992	163499.761/ 145569.916	163253.998/ 145287.284	163257.699/ 145288.802	628.02	4.0	3.5
208	SG/ APS/ B034/ C404/ D405/ 08/ 03	කැටකැරැල්ල හේන්යාය මාර්ගය	163616.035/ 145268.563	163613.876/ 145271.966	164357.348/ 145066.841	164354.49/ 145069.726	961.49	4.0	3.5
209	SG/ APS/ B034/ C404/ D405/ 08/ 03/ 01	හේන්යාය කැටකැරැල්ල පහළ මාර්ගය	163990.074/ 145237.543	163987.423/ 145240.036	163851.196/ 145487.983	163851.066/ 145484.486	364.15	3.5	2.5
210	SG/ APS/ B034/ C404/ D405/ 09	අක්කර 36 පළමු පටුමග	163800.119/ 145712.003	163797.125/ 145714.771	164706.8/ 145736.521	164709.94/ 145738.999	1311.9	4.0	3.5
211	SG/ APS/ B034/ C404/ D405/ 10	අක්කර 36 දෙවන පටුමග	164021.24/ 145639.8	164017.23/ 145641.462	163951.793/ 145849.01	163947.772/ 145849.286	415.39	4.0	3.5
212	SG/ APS/ B034/ C404/ D405/ 11	බදුච්ඡකන්ද ගල්කැරකන්ද මාර්ගය	165014.641/ 145280.167	165015.231/ 145284.137	165346.832/ 145401.242	165346.488/ 145405.227	431.27	4.0	3.5
213	SG/ APS/ B034/ C404/ D405/ 11/ 01	ගල්කැරකන්ද ගලකුර මාර්ගය	165158.3/ 145353.973	165152.821/ 145351.331	166198.582/ 145939.273	166195.509/ 145937.524	1493.5	3.0	2.5

අනු. අංකය	පාලන කේතය	පාලන නම	ආරම්භක බණ්ඩාංක (කදවල ශ්‍රී ලංකා)		අවසාන බණ්ඩාංක (කදවල ශ්‍රී ලංකා)		පාලන දිග (මීටර්)	පාලන පළල (මීටර්)	සංවර්ධන පළල (මීටර්)
			වම	දකුණ	වම	දකුණ			
214	SG/ APS/ B034/ C404/ D405/ 12	බදු වලකන්ද අක්කර 100 අතුරු මාර්ගය	165015.18/ 145244.641	165017.981/ 145242.209	165068.311/ 145044.802	165069.977/ 145046.032	223.49	2.0	1.0
215	SG/ APS/ B034/ C404/ D408/ 01	ලබු ඇල භේන මාර්ගය	160521.458/ 145830.534	160525.82/ 145828.924	160432.723/ 145663.672	160436.722/ 145663.788	281.21	4.0	3.5
216	SG/ APS/ B034/ C404/ D408/ 02	තේ ජනපදය මහින්දාරාමය මාර්ගය	160446.711/ 145882.744	160442.926/ 145885.192	160619.012/ 146203.898	160615.756/ 146202.615	457.76	3.5	3.0
217	SG/ APS/ B034/ C404/ D408/ 02/ 01	තේ ජනපදය මහින්දාරාමය මාර්ගයේ පළමු පටුම	160442.851/ 145922.735	160442.156/ 145926.425	160483.797/ 145913.543	160481.311/ 145916.511	47.94	3.5	3.0
218	SG/ APS/ B034/ C404/ D408/ 02/ 02	තේ ජනපදය මහින්දාරාමය මාර්ගයේ දෙවන පටුම	160436.421/ 145971.767	160435.934/ 145975.38	160544.63/ 145900.79	160546.658/ 145903.644	169.64	3.5	3.0
219	SG/ APS/ B034/ C404/ D408/ 02/ 02/ 01	තේ ජනපදය මහින්දාරාමය මාර්ගයේ දෙවන පටුමෙහි පළමු අතුරු මාර්ගය	160483.556/ 145920.016	160481.336/ 145924.6	160511.205/ 145979.264	160508.558/ 145977.853	77.25	3.0	2.0
220	SG/ APS/ B034/ C404/ D408/ 02/ 03	තේ ජනපදය මහින්දාරාමය මාර්ගයේ තෙවන පටුම	160497.179/ 146104.457	160502.297/ 146106.814	160622.966/ 146038.814	160623.854/ 146042.199	157.01	3.5	3.0
221	SG/ APS/ B034/ C404/ D408/ 02/ 04	තේ ජනපදය මහින්දාරාමය මාර්ගයේ සිව්වන පටුම	160613.368/ 146186.927	160617.507/ 146187.826	160787.105/ 146149.908	160786.575/ 146153.368	189.6	3.5	3.0
222	SG/ APS/ B034/ C404/ D408/ 03	මහින්දාරාමය පළමු පටුම	160355.127/ 146027.079	160352.312/ 146029.781	160402.833/ 146058.487	160403.62/ 146061.383	77.36	3.0	3.0

අනු. අංකය	පාරෙහි කේතය	පාරේ නම	ආරම්භක බණ්ඩංග (කළවල ශ්‍රී ලංකා)		අවසාන බණ්ඩංග (කළවල ශ්‍රී ලංකා)		පාරේ දිග (මීටර්)	පාරේ සාමාන්‍ය පළල (මීටර්)	සංවර්ධිත පළල (මීටර්)
			වම	දකුණ	වම	දකුණ			
223	SG/ APS/ B034/ C404/ D408/ 04	භේවාහැට සමඟි මාවත	160333.715/ 146026.165	160330.912/ 146023.308	159539.665/ 146365.582	159545.419/ 146358.971	1699.4	4.0	3.0
224	SG/ APS/ B034/ C404/ D408/ 04/ 01	භේවාහැට සමඟි මාවතෙහි පළමු පටුම	159844.226/ 146691.312	159841.171/ 146691.491	160035.912/ 146800.095	160032.973/ 146800.693	280.25	3.0	2.5
225	SG/ APS/ B034/ C404/ D408/ 04/ 01/ 01	භේවාහැට සමඟි මාවතෙහි පළමු පටුමගෙහි පළමු අතුරු මාර්ගය	159861.741/ 146731.182	159857.518/ 146729.35	159889.727/ 146770.212	159887.787/ 146770.695	54.14	2.0	2.0
226	SG/ APS/ B034/ C404/ D408/ 04/ 02	භේවාහැට සමඟි මාවතෙහි දෙවන පටුම	159728.552/ 146728.858	159724.349/ 146728.619	159621.929/ 146975.422	159618.476/ 146973.403	477.04	4.0	3.0
227	SG/ APS/ B034/ C404/ D408/ 04/ 02/ 01	භේවාහැට සමඟි මාවතෙහි දෙවන පටුමගෙහි පළමු අතුරු මාර්ගය -අඩි පාර	159684.662/ 146936.945	159685.741/ 146936.62	159659.818/ 146854.201	159660.429/ 146853.41	114.3	1.0	1.0
228	SG/ APS/ B034/ C404/ D408/ 04/ 03	තයදගල පන්සල මාර්ගය	159527.537/ 146619.396	159528.152/ 146616.423	159454.032/ 146835.225	159452.04/ 146837.468	272.6	3.0	3.0
229	SG/ APS/ B034/ C404/ D408/ 05	තේ ජනපදය මානෙල් මාවත	160127.361/ 145996.403	160136.435/ 145993.731	159972.445/ 145325.07	159976.308/ 145326.109	1066.3	4.0	3.0
230	SG/ APS/ B034/ C404/ D408/ 06	පිටකන්ද තේ ජනපදය මාර්ගයේ පළමු පටුම	159935.545/ 146138.611	159931.765/ 146137.118	160021.294/ 146332.061	160017.931/ 146334.367	237.03	4.0	3.0
231	SG/ APS/ B034/ C404/ D408/ 07	පිටකන්ද තේ ජනපදය මාර්ගයේ දෙවන පටුම	159904.209/ 146054.641	159908.641/ 146056.417	159969.111/ 146013.315	159972.1/ 146015.971	80.33	4.0	3.0

අනු-අංකය	පාරෙහි නම	පාරේ නම	ආරම්භක බණ්ඩාංක (කදවල ශ්‍රී ලංකා)		අවසාන බණ්ඩාංක (කදවල ශ්‍රී ලංකා)		පාරේ දිග (මීටර්)	පාරේ සාමාන්‍ය පළල (මීටර්)	සංවර්ධිත පළල (මීටර්)
			වම	දකුණ	වම	දකුණ			
232	SG/ APS/ B034/ C404/ D408/ 08	ජේරගම-ගුවෙ ඇතුළු මාර්ගය	159857.111/ 146242.784	159853.795/ 146244.029	159711.282/ 146499.991	159709.728/ 146496.855	358.11	3.5	2.5
233	SG/ APS/ B034/ C404/ D408/ 09	නේ ජනපදය දිවුල්පොත්ත මාර්ගය	159460.488/ 146382.954	159464.417/ 146384.485	159785.131/ 145677.525	159788.05/ 145679.456	987.55	3.5	2.5
234	SG/ APS/ B034/ C404/ D408/ 10	නේ ජනපදය බටහේන මාර්ගය	159381.228/ 146257.082	159383.543/ 146259.709	158653.716/ 145864.021	158653.703/ 145860.52	1088	3.5	2.5
235	SG/ APS/ B034/ C404/ D408/ 10/ 01	නේ ජනපදය බටහේන මාර්ගයේ පළමු පටුම	159023.381/ 145826.412	159026.802/ 145825.655	159031.943/ 145705.343	159035.056/ 145703.743	128.99	3.5	2.5
236	SG/ APS/ B034/ C404/ D408/ 10/ 02	බටහේන ගඟබඩකැත්ත මාර්ගය	158823.117/ 145833.604	158827.38/ 145833.628	157898.987/ 146369.526	157897.891/ 146365.679	1282	4.0	2.5
237	SG/ APS/ B034/ C404/ D408/ 10/ 02/ 01	බටහේන ගඟබඩකැත්ත මාර්ගයේ පළමු පටුම	158123.941/ 146033.877	158126.979/ 146032.992	158118.056/ 145966	158120.711/ 145967.398	71.9	3.0	2.5
238	SG/ APS/ B034/ C404/ D408/ 10/ 03	බටහේන පන්විලකැත්ත මාර්ගය	158665.833/ 145861.996	158662.019/ 145863.469	158452.434/ 146279.232	158454.773/ 146275.988	640.35	4.0	3.0
239	SG/ APS/ B034/ C404/ D408/ 11	නේ ජනපදය නාමණ්ඩිය මාර්ගය	159260.484/ 146291.527	159260.331/ 146287.138	159027.237/ 146166.165	159026.768/ 146162.697	348.73	3.5	2.5
240	SG/ APS/ B034/ C404/ D408/ 12	කඳුරුවන්දොළ ගලප්පේල මාර්ගය	159290.047/ 146758.405	159287.228/ 146760.688	160057.767/ 147501.851	160054.738/ 147503.62	1411.8	3.5	2.5

අනු. අංකය	පාරෙහි නෝනය	පාරේ නම	ආරම්භක බණ්ඩංක (කළුපිටි ලිංකා)		අවසාන බණ්ඩංක (කළුපිටි ලිංකා)		පාරේ දිග (මීටර්)	පාරේ සාමාන්‍ය පළල (මීටර්)	සංවර්ධිත පළල (මීටර්)
			වම	දකුණ	වම	දකුණ			
241	SG/ APS/ B034/ C404/ D408/13	පිටකන්ද තෙමුගල්පොත්ත ගම්පහ මාර්ගය	158992.757/ 146918.043	158988.008/ 146924.988	159832.598/ 147571.895	159828.886/ 147573.398	1487.5	4.0	2.0
242	SG/ APS/ B034/ C404/ D408/14	පිටකන්ද තලපත්තල ගෙදගල මාර්ගය	158955.393/ 146975.354	158951.401/ 146974.973	156821.817/ 149321.023	156824.14/ 149317.398	4026.87	4.0	2.8
243	SG/ APS/ B034/ C404/ D408/14/ 01	පිටකන්ද තලපත්තල මාර්ගය	158841.061/ 147045.431	158837.28/ 147049.861	158171.437/ 147818.672	158172.122/ 147814.73	1444.73	4.0	2.5
244	SG/ APS/ B034/ C404/ D408/14/ 02	පිටකන්ද තලපත්තල මාර්ගයේ පළමු පටුම	157498.96/ 147878.859	157499.586/ 147874.677	157234.824/ 148089.31	157231.423/ 148087.205	361.03	4.0	2.5
245	SG/ APS/ B034/ C404/ D408/15	පිටකන්ද පළමු පටුම - අඬි පාර	158952.29/ 146786.431	158950.896/ 146783.128	158653.804/ 146783.737	158655.668/ 146779.791	330.99	3.0	2.6
246	SG/ APS/ B034/ C404/ D408/16	පිටකන්ද පන්විලතැන්න මාර්ගය	158992.752/ 146695.263	158995.733/ 146698.178	158585.268/ 146197.093	158584.856/ 146193.067	839.02	4.0	3.0
247	SG/ APS/ B034/ C404/ D408/17	පිටකන්ද මාර්ගයේ දෙවන පටුම	158938.103/ 146697.138	158942.203/ 146696.806	158961.325/ 146672.98	158964.134/ 146674.035	36.88	3.0	2.6
248	SG/ APS/ B034/ C404/ D408/18	පිටකන්ද මාර්ගයේ තෙවන පටුම	158527.876/ 146838.288	158530.889/ 146838.527	158516.682/ 146572.202	158517.281/ 146575.142	301.63	3.0	2.5
249	SG/ APS/ B034/ C404/ D408/19	පිටකන්ද මාර්ගයේ සිව්වන පටුම	158391.624/ 146794.043	158394.664/ 146793.94	158383.118/ 146734.843	158383.936/ 146731.956	68.16	3.0	2.6

අනු-අංකය	පාරමිති නිකේතය	පාරම්‍ය නම	ආරම්භක බණ්ඩාංක (කදවල ශ්‍රී ලංකා)		අවසාන බණ්ඩාංක (කදවල ශ්‍රී ලංකා)		පාරේ දිග (මීටර්)	පාරේ සාමාන්‍ය පළල (මීටර්)	සංවර්ධිත පළල (මීටර්)
			වම	දකුණ	වම	දකුණ			
250	SG/ APS/ B034/ C404/ D408/20	පිටකන්ද මාර්ගයේ පස්වන පටුම	158371.028/ 146839.404	158370.205/ 146841.229	158389.514/ 146863.734	158387.878/ 146864.886	33.99	2.0	1.6
251	SG/ APS/ B034/ C404/ D408/21	පිටකන්ද මාර්ගයේ සයවන පටුම	158320.446/ 146865.636	158314.122/ 146867.684	157949.878/ 146559.532	157951.843/ 146556.634	1178.49	3.5	3.0
252	SG/ APS/ B034/ C404/ D408/ 21/ 01	පිටකන්ද මාර්ගයේ සයවන පටුමගේ පළමු අතුරු මාර්ගය- අඩි පාර	157801.663/ 147049.828	157798.386/ 147047.874	157712.91/ 147152.417	157710.026/ 147153.239	165.53	3.0	2.5
253	SG/ APS/ B034/ C404/ D408/ 22	පිටකන්ද ගම්පහ අඩි පාර	158185.44/ 146770.019	158188.761/ 146770.059	157934.147/ 146347.428	157935.373/ 146343.932	545.86	3.0	1.6
254	SG/ APS/ B034/ C404/ D408/ 23	පිටකන්ද මාර්ගයේ සත්වන පටුම	158184.025/ 146774.431	158185.44/ 146770.019	157856.121/ 146923.467	157860.114/ 146923.231	434.81	4.0	1.0
255	SG/ APS/ B034/ C404/ D406/ 01	අඹගහ හංදිය කළුමැදිය මාර්ගය	161131.443/ 145171.071	161134.896/ 145173.252	162750.019/ 144418.317	162752.289/ 144421.611	2582.81	4.0	3.0
256	SG/ APS/ B034/ C404/ D406/ 01/ 01	කළුමැදිය මාර්ගයේ පළමු පටුම	162224.666/ 144453.272	162227.802/ 144450.355	162240.579/ 144363.174	162241.403/ 144366.058	103.38	3.0	2.5
257	SG/ APS/ B034/ C404/ D406/ 01/ 02	කළුමැදිය නේ කන්ද කුට්ටිකන්ද මාර්ගය	162264.039/ 144484.394	162260.383/ 144487.966	164605.873/ 142928.664	164610.047/ 142928.024	3867.5	4.0	3.0
258	SG/ APS/ B034/ C404/ D406/ 01/ 02/ 01	කළුමැදිය නේ කන්ද කුට්ටිකන්ද මාර්ගයේ පළමු පටුම	164581.481/ 143010.128	164579.459/ 143013.662	164648.764/ 143122.174	164646.671/ 143125.582	137.74	4.0	3.0

අනු. අංකය	පාරෙහි නොය	පාරේ නම	ආරම්භක බණ්ඩංග (කළුපිලි ලංකා)		අවසාන බණ්ඩංග (කළුපිලි ලංකා)		පාරේ දිග (මීටර්)	පාරේ සාමාන්‍ය පළල (මීටර්)	සංවර්ධිත පළල (මීටර්)
			වම	දකුණ	වම	දකුණ			
259	SG/ APS/ B034/ C404/ D406/ 01/ 03	කළුමැදිය මාර්ගයේ දෙවන පටුම	162112.541/ 144752.893	162110.722/ 144749.256	161559.35/ 145069.992	161557.014/ 145066.745	667.89	4.0	3.5
260	SG/ APS/ B034/ C404/ D406/ 01/ 04	කළුමැදිය මාර්ගයේ තෙවන පටුම	162123.865/ 144753.511	162126.766/ 144755.492	162212.608/ 144716.623	162213.008/ 144720.099	99.83	3.5	3.0
261	SG/ APS/ B034/ C404/ D406/ 01/ 05	කළුමැදිය මාර්ගයේ සිව්වන පටුම	162370.841/ 144695.009	162366.643/ 144697.738	162578.124/ 144642.282	162581.031/ 144644.23	244.7	3.5	3.0
262	SG/ APS/ B034/ C404/ D406/ 02	අඹගහ හංදිය ගමියා මාර්ගය	161135.019/ 145178.676	161132.62/ 145175.212	161022.205/ 145644.805	161019.354/ 145641.999	557.3	4.0	2.5
263	SG/ APS/ B034/ C404/ D406/ 03	හැරැස්ස ගමිකන්දෙත්ත මාර්ගය	161605.18/ 145371.611	161608.64/ 145371.892	162768.247/ 144927.2	162765.285/ 144927.678	1417.51	3.0	2.5
264	SG/ APS/ B034/ C404/ D406/ 03/ 01	හැරැස්ස ගමිකන්දෙත්ත මාර්ගයේ පළමු පටුම	161723.374/ 145276.48	161725.7/ 145273.754	161612.773/ 145238.659	161612.75/ 145235.159	125.73	3.5	3.0
265	SG/ APS/ B034/ C404/ D406/ 03/ 02	හැරැස්ස ගමිකන්දෙත්ත කළුමැදිය මාර්ගය	162368.317/ 144896.297	162375.609/ 144893.679	162499.257/ 144666.71	162502.681/ 144664.757	298.32	3.5	2.0
266	SG/ APS/ B034/ C404/ D406/ 04	දිග්ගල හැරැස්ස පළමු පටුම	161757.972/ 145517.095	161753.657/ 145517.637	161631.558/ 145673.812	161634.352/ 145672.721	324.09	3.0	2.5
267	SG/ APS/ B034/ C404/ D406/ 05	දිග්ගල හැරැස්ස දෙවන පටුම	161830.27/ 145488.7	161827.098/ 145490.218	161859.82/ 145549.14	161857.127/ 145551.377	70.26	3.5	3.0

අනු. අංකය	පාලනික කේතය	පාලන නම	ආරම්භක බණ්ඩාංක (කදවල ශ්‍රී ලංකා)		අවසාන බණ්ඩාංක (කදවල ශ්‍රී ලංකා)		පාලන දිග (මීටර්)	පාලන සාමාන්‍ය පළල (මීටර්)	සංවර්ධන පළල (මීටර්)
			වම	දකුණ	වම	දකුණ			
268	SG/ APS/ B034/ C404/ D406/ 06	දිග්ගල හැඳුණු තෙවන පවුම	162188.258/ 145563.453	162185.755/ 145561.775	161942.929/ 145692.707	161939.989/ 145693.305	307	3.0	2.5
269	SG/ APS/ B034/ C404/ D406/ 07	ගම්කන්ද පල්ලෙකඩ මාර්ගය	162742.986/ 145275.341	162740.918/ 145278.928	162286.339/ 145870.993	162287.869/ 145867.297	976.53	4.0	3.0
270	SG/ APS/ B034/ C404/ D406/ 07/ 01	ගම්කන්ද පල්ලෙකඩ මාර්ගයේ පළමු පවුම	162807.26/ 145344.143	162810.308/ 145346.885	162934.139/ 145311.753	162930.158/ 145312.137	163.63	4.0	2.5
271	SG/ APS/ B034/ C404/ D406/ 08	හැඳුණු අක්කර 20 මාර්ගය	162781.233/ 145178.911	162783.57/ 145175.794	163371.974/ 144353.077	163372.966/ 144350.245	1227.93	3.0	2.5
272	SG/ APS/ B034/ C404/ D406/ 08/ 01	හැඳුණු අක්කර 20 ගල්පොත්ත මාර්ගය	163169.07/ 144636.912	163172.194/ 144635.587	163154.466/ 144365.837	163156.867/ 144367.636	449.28	3.0	2.5
273	SG/ APS/ B034/ C404/ D406/ 09	දිග්ගල හැඳුණු මාර්ගය	162982.034/ 145043.287	162978.825/ 145045.674	163923.35/ 144979.121	163920.473/ 144982.068	1085.36	4.0	3.0
274	SG/ APS/ B034/ C404/ D406/ 09/ 01	දිග්ගල මුකලාන මාර්ගය	163169.314/ 145100.199	163169.314/ 145100.199	163056.984/ 145390.869	163054.742/ 145388.875	379.65	3.0	2.0
275	SG/ APS/ B034/ C404/ D406/ 10	දිග්ගල හැඳුණු සිව්වන පවුම	163495.456/ 144665.743	163490.517/ 144667.758	163580.059/ 144758.336	163580.113/ 144761.836	232.18	3.5	2.5
276	SG/ APS/ B034/ C404/ D406/ 11	දිග්ගල හැඳුණු අතුරු මාර්ගය -අඩි පාර	163662.368/ 144590.539	163660.819/ 144591.402	163837.071/ 144889.362	163836.118/ 144888.003	405.69	1.5	1.0

අනු. අංකය	පාරෙහි කෝනය	පාරේ නම	ආරම්භක බණ්ඩංක (කළුල ශ්‍රී ලංකා)		අවසාන බණ්ඩංක (කළුල ශ්‍රී ලංකා)		පාරේ දිග (මීටර්)	පාරේ සාමාන්‍ය පළල (මීටර්)	සංවර්ධිත පළල (මීටර්)
			වම	දකුණ	වම	දකුණ			
277	SG/ APS/ B034/ C404/ D406/ 12	කුට්ටිකන්ද මාර්ගය	163664.449/ 144585.944	163667.172/ 144584.426	164044.067/ 144246.188	164044.113/ 144249.187	806.19	3.0	3.0
278	SG/ APS/ B034/ C404/ D406/ 12/ 01	කුට්ටිකන්ද උම්ංආල මාර්ගය	163639.496/ 144482.403	163639.278/ 144479.904	163494.483/ 144343.5	163496.523/ 144344.945	256.78	2.5	2.0
279	SG/ APS/ B034/ C404/ D407/ 01	ගවරගිටිය වෙල්මණ්ඩිය හරහා මුනිකන්ද මාර්ගයේ පළමු පටුම	160699.858/ 143935.506	160703.361/ 143935.567	160661.878/ 143848.602	160664.132/ 143845.925	105.65	3.5	3.0
280	SG/ APS/ B034/ C404/ D407/ 02	ගවරගිටිය කොළඹුව මාර්ගය	160327.199/ 143850.242	160329.754/ 143845.734	158174.679/ 143543.167	158176.11/ 143540.53	4713.83	3.0	2.8
281	SG/ APS/ B034/ C404/ D407/ 02/ 01	ගම්වසම පළමු පටුම	160148.25/ 143158.168	160149.739/ 143161.848	160251.028/ 143076.245	160254.979/ 143076.863	140.62	4.0	3.0
282	SG/ APS/ B034/ C404/ D407/ 02/ 02	තැබ්බකන්ද මාර්ගය	159992.397/ 143096.675	159988.046/ 143097.569	158432.198/ 143398.985	158433.316/ 143395.136	2083.16	4.0	3.0
283	SG/ APS/ B034/ C404/ D407/ 02/ 02/ 01	කොඳුගල මාර්ගය	158669.768/ 143759.738	158673.128/ 143762.179	158169.001/ 143726.865	158173.893/ 143724.586	1119.83	4.0	3.0
284	SG/ APS/ B034/ C404/ D407/ 02/ 02/ 02	තැබ්බකන්ද මාර්ගයේ පළමු පටුම	158454.333/ 143404.292	158459.596/ 143408.227	158565.735/ 143409.54	158564.696/ 143413.403	113.2	4.0	3.0
285	SG/ APS/ B034/ C404/ D407/ 02/ 03	නිශ්ගම බුලත්භිංහල මාර්ගය	159860.232/ 142810.67	159869.03/ 142810.453	160719.397/ 142209.444	160720.446/ 142213.304	1113.02	4.0	3.0

අනු. අංකය	පාරමිති කේතය	පාරමිති නම	ආරම්භක බණ්ඩාංක (කදවල ශ්‍රී ලංකා)		අවසාන බණ්ඩාංක (කදවල ශ්‍රී ලංකා)		පාරමිති දිග (මීටර්)	පාරමිති සාමාන්‍ය පළල (මීටර්)	සංවර්ධිත පළල (මීටර්)
			වම	දකුණ	වම	දකුණ			
286	SG/ APS/ B034/ C404/ D407/ 02/ 03/ 01	නිශ්චල බුලත්කිංචල මාර්ගයේ පළමු පටුම	160588.267/ 142272.567	160586.011/ 142274.583	160721.102/ 142641.984	160721.439/ 142644.966	924.49	3.0	2.6
287	SG/ APS/ B034/ C404/ D407/ 02/ 04	ගම්බල බණ්ඩිය නැඟිකන්ද මාර්ගය	159758.823/ 142781.741	159754.918/ 142780.886	159730.077/ 143276.113	159727.642/ 143278.002	1077.1	3.0	3.0
288	SG/ APS/ B034/ C404/ D407/ 02/ 05	ගවරගිරිය කොළඹුව මාර්ගයේ පළමු පටුම	159720.815/ 142722.739	159720.174/ 142719.347	159357.438/ 142973.765	159359.763/ 142971.87	515.98	3.0	2.7
289	SG/ APS/ B034/ C404/ D407/ 02/ 06	ගවරගිරිය කොළඹුව මාර්ගයේ දෙවන පටුම	158383.129/ 143228.229	158383.713/ 143232.571	158576.865/ 143284.811	158574.171/ 143288.034	237.37	4.2	2.8
290	SG/ APS/ B034/ C404/ D407/ 02/ 07	ගවරගිරිය කොළඹුව මාර්ගයේ තෙවන පටුම	158282.665/ 143540.767	158278.032/ 143541.949	158197.617/ 144086.884	158196.338/ 144089.597	652.69	3.0	3.0
291	SG/ APS/ B034/ C404/ D407/ 03	ගවරගිරිය මුනිකන්ද මාර්ගයේ පළමු පටුම	160070.308/ 144121.318	160074.095/ 144115.104	159968.153/ 144113.02	159970.943/ 144111.919	150.67	3.0	2.5
292	SG/ APS/ B034/ C404/ D407/ 04	ගවරගිරිය මුනිකන්ද මාර්ගයේ දෙවන පටුම	159794.826/ 144264.634	159797.389/ 144263.063	159768.364/ 144244.475	159770.02/ 144241.973	36.26	3.0	2.5
293	SG/ APS/ B034/ C404/ D407/ 05	ගවරගිරිය මුනිකන්ද මාර්ගයේ තෙවන පටුම	159666.649/ 144453.8	159663.63/ 144455.816	159807.424/ 144467.393	159805.364/ 144469.573	164.01	3.0	2.5

අනු. අංකය	පාරෙහි කෝනය	පාරේ නම	ආරම්භක බණ්ඩාංක (කළුපිලි ලංකා)		අවසාන බණ්ඩාංක (කළුපිලි ලංකා)		පාරේ දිග (මීටර්)	පාරේ සාමාන්‍ය පළල (මීටර්)	සංවර්ධිත පළල (මීටර්)
			වම	දකුණ	වම	දකුණ			
294	SG/ APS/ B034/ C404/ D407/ 06	ගවරගිරිය මුනිනිකන්ද මාර්ගයේ සිව්වන පටුම	159448.12/ 144509.898	159444.09/ 144510.486	159608.707/ 144592.149	159610.995/ 144595.43	316.5	4.0	3.0
295	SG/ APS/ B034/ C404/ D407/ 06/ 01	ගවරගිරිය මුනිනිකන්ද මාර්ගයේ සිව්වන පටුමගෙහි පළමු අතුරු මාර්ගය	159546.329/ 144610.2	159541.403/ 144611.997	159544.549/ 144642.438	159540.597/ 144643.056	35.18	4.0	3.0
296	SG/ APS/ B034/ C404/ D407/ 07	කොළඹුව මුනිනිකන්ද ඉහළ කන්ද මාර්ගය	158971.526/ 144597.328	158969.03/ 144594.416	158120.112/ 145533.83	158116.754/ 145532.053	1357.1	3.8	3.0
297	SG/ APS/ B034/ C404/ D407/ 07/ 01	කොළඹුව මුනිනිකන්ද ඉහළ කන්ද මාර්ගයේ පළමු පටු මාර්ගය	158847.003/ 144733.997	158845.258/ 144738.239	159039.194/ 144981.19	159036.634/ 144983.272	428.42	3.3	3.0
298	SG/ APS/ B034/ C404/ D407/ 07/ 02	කොළඹුව මුනිනිකන්ද දෙවැනි මට්ටමේ මාර්ගය	158696.391/ 144884.86	158699.492/ 144883.193	158634.513/ 144675.817	158636.259/ 144678.85	242.44	3.5	2.8
299	SG/ APS/ B034/ C404/ D407/ 07/ 03	කොළඹුව මුනිනිකන්ද පස්වන පටුම	158542.604/ 145028.014	158538.637/ 145030.686	158714.365/ 145131.924	158714.169/ 145134.917	392.11	3.0	2.5
300	SG/ APS/ B034/ C404/ D407/ 07/ 03/ 01	කොළඹුව මුනිනිකන්ද පස්වන පටුමගෙහි පළමු අතුරු මාර්ගය	158590.991/ 145201.086	158587.689/ 145201.461	158695.52/ 145353.7	158696.379/ 145356.574	601.07	3.0	2.5
301	SG/ APS/ B034/ C404/ D407/ 08	කොළඹුව මුනිනිකන්ද සයවන පටුම	158866.522/ 144388.389	158865.883/ 144385.255	158610.211/ 144338.245	158608.168/ 144336.049	291.71	3.0	2.5
302	SG/APS/B034/C404/ C401/01	ලන්දේලියේ මාර්ගය	163569.417/ 141308.403	163565.619/ 141309.094	163332.674/ 141668.101	163331.132/ 141664.958	469.6	3.5	2.5

අනු-අංකය	පාලන නිකේතය	පාලන නම	ආරම්භක බණ්ඩාංක (කදවල ශ්‍රී ලංකා)		අවසාන බණ්ඩාංක (කදවල ශ්‍රී ලංකා)		පාලන දිග (මීටර්)	පාලන සාමාන්‍ය පළල (මීටර්)	සංවර්ධන පළල (මීටර්)
			වම	දකුණ	වම	දකුණ			
303	SG/ APS/ B034/ C404/ C401/ 02	දුම්රිය මාර්ගය කළුතර මාර්ගය	163944.518/ 141303.777	163948.493/ 141304.248	166245.219/ 139702.94	166244.348/ 139706.936	3549.34	4.0	3.5
304	SG/ APS/ B034/ C404/ C401/ 02/ 01	මහවැලිපිටිය පහළ පළමු මාර්ගය	166002.781/ 139632.525	166010.627/ 139627.027	164611.691/ 139486.328	164611.307/ 139482.347	1750.26	4.0	2.5
305	SG/ APS/ B034/ C404/ C401/ 02/ 01/ 01	මහවැලිපිටිය බටහිර පළමු මාර්ගය	165888.461/ 139579.195	165892.671/ 139580.48	165866.895/ 139267.512	165870.825/ 139266.768	458.09	4.0	3.0
306	SG/ APS/ B034/ C404/ C401/ 02/ 01/ 02	මහවැලිපිටිය පහළ දෙවන මාර්ගය	165627.987/ 139570.743	165623.85/ 139571.777	165642.93/ 139611.545	165640.391/ 139614.636	48.85	4.0	3.0
307	SG/ APS/ B034/ C404/ C401/ 02/ 01/ 03	මහවැලිපිටිය බටහිර දෙවන මාර්ගය	165489.395/ 139597.805	165494.258/ 139595.241	165390.308/ 139350.989	165393.146/ 139353.809	406.11	4.0	2.5
308	SG/ APS/ B034/ C404/ C401/ 02/ 01/ 04	මහවැලිපිටිය පහළ තෙවන මාර්ගය	165321.014/ 139668.669	165316.721/ 139668.115	165302.971/ 139736.613	165299.871/ 139734.989	72.95	3.5	2.5
309	SG/ APS/ B034/ C404/ C401/ 02/ 01/ 05	සෝදුරුකන්ද මාර්ගය	164924.12/ 139470.482	164918.59/ 139471.973	164709.911/ 139695.183	164708.337/ 139691.506	434.5	4.0	2.5
310	SG/ APS/ B034/ C404/ C401/ 02/ 02	දුම්රිය අංක 02 මාර්ගය	166065.85/ 139574.914	166069.315/ 139571.639	167182.273/ 138722.521	167178.712/ 138720.7	2153.7	4.0	2.5
311	SG/ APS/ B034/ C404/ C401/ 02/ 02/ 01	දුම්රිය අංක 02 මාර්ගයේ පළමු පටුම	166130.695/ 139486.064	166134.467/ 139484.669	166278.353/ 139166.614	166282.224/ 139165.607	384.13	4.0	2.5
312	SG/ APS/ B034/ C404/ C401/ 02/ 02/ 01/ 01	දුම්රිය අංක 02 මාර්ගයේ පළමු පටුමෙහි පළමු අතුරු මාර්ගය	166146.247/ 139397.065	166152.835/ 139391.805	166076.601/ 139392.33	166075.03/ 139389.773	127.38	3.0	2.5

අනු. අංකය	පාලන ඒකකය	පාරේ නම	ආරම්භක බණ්ඩංග (කළුපිට ලංකා)		අවසාන බණ්ඩංග (කළුපිට ලංකා)		පාරේ දිග (මීටර්)	පාරේ පළල (මීටර්)	සංවර්ධන පළල (මීටර්)
			වම	දකුණ	වම	දකුණ			
313	SG/ APS/ B034/ C404/ C401/ 03	දුම්රිය මාර්ගය	164164.67/ 141345.967	164158.941/ 141346.65	165891.23/ 142114.353	165896.228/ 142114.522	5413.5	5.0	2.5
314	SG/ APS/ B034/ C404/ C401/ 03/ 01	අංක 01 දුම්රිය මාර්ගය	164536.479/ 141436.909	164537.5/ 141440.87	167409.194/ 139926.99	167413.289/ 139928.864	3909.5	4.0	2.5
315	SG/ APS/ B034/ C404/ C401/ 03/ 02	දුම්රිය මාර්ගය	164380.898/ 141542.213	164377.625/ 141544.513	164052.052/ 142374.41	164051.034/ 142370.542	1216.5	4.0	2.6
316	SG/ APS/ B034/ C404/ C401/ 03/ 02/ 01	දුම්රිය මාර්ගය	164459.644/ 141680.811	164456.362/ 141678.194	164138.131/ 141911.672	164137.558/ 141907.714	427.07	4.0	3.0
317	SG/ APS/ B034/ C404/ C401/ 03/ 02/ 02	දුම්රිය මාර්ගය	164531.977/ 141828.718	164529.88/ 141831.622	164643.566/ 142030.531	164640.092/ 142030.108	257.64	3.5	2.5
318	SG/ APS/ B034/ C404/ C401/ 03/ 02/ 02/ 01	දුම්රිය මාර්ගය	164636.291/ 141954.722	164634.939/ 141959.151	165198.71/ 141807.634	165202.07/ 141804.641	631.81	4.5	2.5
319	SG/ APS/ B034/ C404/ C401/ 03/ 02/ 03	දුම්රිය මාර්ගය	164258.957/ 142003.341	164262.152/ 141997.765	164100.798/ 142116.06	164099.281/ 142112.905	209.33	3.5	2.5
320	SG/ APS/ B034/ C404/ C401/ 03/ 03	දුම්රිය මාර්ගය	163635.671/ 142357.046	163633.06/ 142355.555	163354.38/ 142662.842	163352.065/ 142660.933	437.79	3.0	2.5
321	SG/ APS/ B034/ C404/ C401/ 03/ 04	දුම්රිය මාර්ගය	163841.381/ 142762.389	163843.517/ 142765.997	164050.29/ 142644.156	164052.236/ 142640.66	284.95	4.0	2.6

අනු. අංකය	පාලන නිකේතය	පාලන නම	ආරම්භක බණ්ඩාංක (කදවල ශ්‍රී ලංකා)		අවසාන බණ්ඩාංක (කදවල ශ්‍රී ලංකා)		පාලන දිග (මීටර්)	පාලන සාමාන්‍ය පළල (මීටර්)	සංවර්ධන පළල (මීටර්)
			වම	දකුණ	වම	දකුණ			
322	SG/ APS/ B034/ C404/ C401/ 03/ 05	දුම්රිය මාර්ගය කුට්ටිකන්ද මාර්ගයේ දෙවන පටු මාර්ගය	164428.871/ 142945.801	164432.902/ 142942.32	164393.2/ 142868.601	164393.885/ 142864.66	122.87	4.0	3.0
323	SG/ APS/ B034/ C404/ C401/ 04	අංක 82 කෙස්විල අසල මාර්ගය	166942.524/ 139483.98	166935.276/ 139486.901	167628.782/ 139477.376	167628.157/ 139480.819	733.48	3.5	2.5
324	SG/ APS/ B034/ C404/ C401/ 05	දුම්රිය අංක 82 අඩි පාර	167105.569/ 139423.374	167107.583/ 139422.322	167227.378/ 138954.551	167229.145/ 138955.489	777.67	2.0	1.5
325	SG/ APS/ B034/ C404/ C401/ 06	දුම්රිය අංක 01 මාර්ගය	168182.573/ 138870.069	168182.06/ 138874.932	167809.426/ 140441.934	167805.474/ 140442.553	2313.73	4.0	3.0
326	SG/ APS/ B034/ C404/ C401/ 07	දුම්රිය මැදිකැල්ල ඉහළ මාර්ගය	168219.125/ 138592.16	168214.867/ 138602.546	168972.466/ 138633.193	168973.006/ 138637.156	1081.8	4.0	2.5
327	SG/ APS/ B034/ C404/ C401/ 08	මිණිපුර දුම්රිය මාර්ගය	168635.217/ 138228.821	168631.853/ 138226.142	168544.386/ 138262.959	168540.747/ 138261.297	115.54	4.0	3.0
328	SG/ APS/ B034/ C404/ C401/ 09	මිණිපුර දුම්රිය අටහෙරලියගොඩ මාර්ගය	168751.409/ 138073.939	168755.543/ 138073.175	168033.794/ 138501.759	168029.868/ 138502.53	1095.3	4.0	2.6
329	SG/ APS/ B034/ C404/ C401/ 10	පැණිගලවත්ත තොටුපොළ මාර්ගය	168799.218/ 137902.52	168802.731/ 137898.96	170067.609/ 137559.462	170064.276/ 137563.216	4084.9	5.0	2.6
330	SG/ APS/ B034/ C404/ C401/ 10/ 01	දුම්රිය කඩවල මාර්ගය	168157.401/ 137774.094	168157.087/ 137769.89	167997.597/ 138114.812	167995.529/ 138117.635	472.76	3.5	2.5

අනු. අංකය	පාරෙහි නේතය	පාරේ නම	ආරම්භක බණ්ඩංක (කළුපිලි ලංකා)		අවසාන බණ්ඩංක (කළුපිලි ලංකා)		පාරේ දිග (මීටර්)	පාරේ සාමාන්‍ය පළල (මීටර්)	සංවර්ධිත පළල (මීටර්)
			වම	දකුණ	වම	දකුණ			
331	SG/ APS/ B034/ C404/ C401/ 10/ 02	පැණිගලවත්ත තොටුපොළ මාර්ගයේ පළමු පටුම	168309.105/ 137506.554	168316.913/ 137504.135	168229.945/ 137508.79	168226.846/ 137506.262	98.39	4.0	3.0
332	SG/ APS/ B034/ C404/ C401/ 10/ 03	පැණිගලවත්ත හල්වතුර මාර්ගය	168712.289/ 137288.585	168716.23/ 137284.514	168665.296/ 137188.45	168669.989/ 137186.726	115.29	5.0	2.6
333	SG/ APS/ B034/ C404/ C401/ 10/ 04	පැණිගලවත්ත තොටුපොළ මාර්ගයේ දෙවන පටුම	168947.665/ 137212.914	168953.147/ 137210.257	168966.707/ 137126.2	168969.474/ 137128.342	101.26	3.5	2.0
334	SG/ APS/ B034/ C404/ C401/ 10/ 05	පැණිගලවත්ත තොටුපොළ මාර්ගයේ තෙවන පටුම	169420.173/ 137141.16	169423.788/ 137141.825	169384.294/ 136898.167	169387.592/ 136899.342	257.57	3.5	2.5
335	SG/ APS/ B034/ C404/ C401/ 10/ 06	පැණිගලවත්ත තොටුපොළ මාර්ගයේ සිව්වන පටුම	169946.902/ 137056.331	169951.315/ 137055.014	169858.152/ 136653.153	169858.993/ 136649.243	651.13	4.0	2.1
336	SG/ APS/ B034/ C404/ C401/ 10/ 07	පැණිගලවත්ත තොටුපොළ මාර්ගයේ පස්වන පටුම	169954.559/ 137054.354	169959.449/ 137054.23	170064.331/ 136947.26	170068.922/ 136946.957	176.83	4.6	4.0
337	SG/ APS/ B034/ C404/ C401/ 11	දොම්භියාවත්ත තොටුපොළ මාර්ගය	169590.917/ 138087.129	169585.055/ 138097.712	170081.326/ 137540.973	170084.233/ 137543.72	988.19	4.0	2.5
338	SG/ APS/ B034/ C404/ C401/ 12	මැදපොළ අංක 01 මාර්ගය	169568.796/ 138653.691	169568.472/ 138644.097	167450.006/ 139959.141	167446.501/ 139953.649	2699.67	3.5	2.5
339	SG/ APS/ B034/ C404/ C401/ 13	පහළපොළ පළමු මාර්ගය	169603.301/ 138783.925	169616.912/ 138787.77	169853.565/ 138550.38	169855.909/ 138554.916	366.21	5.0	2.5

අනු-අංකය	පාරමිති කේතය	පාරමිති නම	ආරම්භක බණ්ඩාංක (කදවල ශ්‍රී ලංකා)		අවසාන බණ්ඩාංක (කදවල ශ්‍රී ලංකා)		පාරමිති දිග (මීටර්)	පාරමිති පළල (මීටර්)	සංවර්ධිත පළල (මීටර්)
			වම	දකුණ	වම	දකුණ			
340	SG/ APS/ B034/ C404/ C401/ 14	පහළපොළ දෙවන මාර්ගය	169959.605/ 138553.252	169964.691/ 138549.087	170148.286/ 138438.809	170149.175/ 138442.708	455.02	4.0	3.0
341	SG/ APS/ B034/ C404/ C401/ 14/ 01	පහළපොළ දෙවන මාර්ගයේ පළමු පටුම	169880.599/ 138506.303	169884.09/ 138506.695	170065.251/ 138101.546	170068.631/ 138102.455	515.72	3.5	2.5
342	SG/ APS/ B034/ C404/ C401/ 14/ 02	පහළපොළ දෙවන මාර්ගයේ දෙවන පටුම	170042.718/ 138459.316	170045.674/ 138458.35	170006.107/ 138388.362	170008.808/ 138386.793	87.99	3.0	2.0
343	SG/ APS/ B034/ C404/ C401/ 14/ 03	පහළපොළ දෙවන මාර්ගයේ තෙවන පටුම	170120.979/ 138439.662	170123.481/ 138439.708	170025.403/ 138374.488	170027.377/ 138372.639	135.11	2.5	2.5
344	SG/ APS/ B034/ C404/ C401/ 15	පහළපොළ තෙවන මාර්ගය	170094.887/ 138614.153	170098.645/ 138615.552	170189.197/ 138604.204	170185.914/ 138606.488	120.09	4.0	2.5
345	SG/ APS/ B034/ C404/ C401/ 15/ 01	පහළපොළ තෙවන මාර්ගයේ පළමු පටුම	170108.994/ 138589.081	170111.809/ 138586.657	170121.508/ 138443.672	170124.792/ 138443.741	163.95	3.0	2.5
346	SG/ APS/ B034/ C402/ 01	අයගම ඇලපාන මාර්ගයේ පළමු මාර්ගය	159461.777/ 149379.181	159458.973/ 149381.326	159387.298/ 149574.851	159385.347/ 149571.943	256.14	3.5	3.0
347	SG/ APS/ B034/ C402/ 01/ 01	අයගම ඇලපාන මාර්ගයේ පළමු මාර්ගයේ පළමු අතුරු මාර්ගය	159423.585/ 149522.478	159424.399/ 149525.883	159502.077/ 149478.071	159503.732/ 149481.156	93.1	3.5	3.0
348	SG/ APS/ B034/ C402/ 02	සරත්චන්ද්‍රය මැද මාර්ගය	159447.649/ 149388.194	159450.001/ 149384.943	159232.965/ 149320.121	159236.74/ 149318.507	300.32	4.0	3.0
349	SG/ APS/ B034/ C402/ 02/ 01	සරත්චන්ද්‍රය මැද මාර්ගයේ පළමු පටුම	159382.923/ 149306.953	159382.727/ 149304.453	159306.148/ 149352.255	159304.278/ 149350.595	93.78	2.5	1.0

අනු. අංකය	පාරෙහි කේතය	පාරේ නම	ආරම්භක බණ්ඩංක (කළුපිටි ලංකා)		අවසාන බණ්ඩංක (කළුපිටි ලංකා)		පාරේ දිග (මීටර්)	පාරේ සාමාන්‍ය පළල (මීටර්)	සංවර්ධිත පළල (මීටර්)
			වම	දකුණ	වම	දකුණ			
350	SG/ APS/ B034/ C402/ 02/ 02	සරත්පුරය මැද මාර්ගයේ දෙවන පටුමග	159255.574/ 149335.976	159252.454/ 149334.811	159277.353/ 149390.737	159276.866/ 149393.697	66.48	3.0	3.0
351	SG/ APS/ B034/ C402/ 03	සරත්පුරය පළමු පටුමග	159381.676/ 149465.264	159383.42/ 149462.67	159240.917/ 149429.631	159241.003/ 149426.547	155.78	3.0	3.0
352	SG/ APS/ B034/ C402/ 04	අයගම ඇලපාන මාර්ගයේ දෙවන මාර්ගය	159389.948/ 149582.055	159387.143/ 149580.654	159326.662/ 149723.997	159323.688/ 149723.605	197.56	3.0	3.0
353	SG/ APS/ B034/ C402/ 05	අයගම ඇලපාන මාර්ගයේ තෙවන මාර්ගය	159537.463/ 149681.071	159537.114/ 149684.57	159592.073/ 149643.185	159591.783/ 149646.672	75.32	3.5	3.5
354	SG/ APS/ B034/ C402/ 06	අයගම ඇලපාන මාර්ගයේ සිව්වන මාර්ගය	159510.747/ 149768.346	159511.485/ 149764.748	159257.203/ 149882.453	159256.039/ 149879.153	316.02	3.5	3.5
355	SG/ APS/ B034/ C402/ 07	සමරුගම මැද මාර්ගය	159379.418/ 149957.766	159379.92/ 149954.302	159165.735/ 149699.736	159169.01/ 149701.016	493.07	3.5	3.0
356	SG/ APS/ B034/ C402/ 08	අයගම ඇලපාන මාර්ගයේ පස්වන මාර්ගය	159279.654/ 150104.126	159277.422/ 150106.134	159689.449/ 149943.843	159686.7/ 149945.045	505.46	3.0	3.0
357	SG/ APS/ B034/ C402/ 09	අයගම ඇලපාන මාර්ගයේ සයවන මාර්ගය	159128.731/ 150373.43	159126.751/ 150370.511	158792.732/ 150542.001	158795.844/ 150540.399	578.75	3.5	3.0
358	SG/ APS/ B034/ C402/ 10	අයගම ඇලපාන මාර්ගයේ සත්වන මාර්ගය	159741.171/ 150667.187	159740.058/ 150670.378	160130.92/ 150920.892	160129.531/ 150923.551	613.49	3.0	3.0


අනු-අංකය	පාරමිති කේතය	පාරමිති	ආරම්භක බණ්ඩාංක (කදවල ශ්‍රී ලංකා)		අවසාන බණ්ඩාංක (කදවල ශ්‍රී ලංකා)		පාරමිති දිග (මීටර්)	පාරමිති පළල (මීටර්)	සංවර්ධන පළල (මීටර්)
			වම	දකුණ	වම	දකුණ			
359	SG/ APS/ B034/ D401/ 01	පළමු ගෙදර මාර්ගය	157287.745/ 150320.142	157291.64/ 150321.053	156313.654/ 146716.075	156316.312/ 146713.085	5197.6	4.0	3.5
360	SG/ APS/ B034/ D401/ 01/ 01	තැන්පත් වන මාර්ගය	157208.055/ 150206.886	157209.151/ 150203.024	156709.13/ 150088.967	156713.044/ 150089.79	1057.6	4.0	4.0
361	SG/ APS/ B034/ D401/ 01/ 02	තැන්පත් ජනපදය මාර්ගය	157320.013/ 149886.172	157317.269/ 149883.871	156982.264/ 149661.686	156985.239/ 149659.842	566.71	3.5	3.0
362	SG/ APS/ B034/ D401/ 01/ 02/ 01	තැන්පත් ඉහළ මාර්ගය	157227.648/ 149894.143	157225.013/ 149892.709	157160.356/ 149888.568	157163.081/ 149887.312	95.31	3.0	3.0
363	SG/ APS/ B034/ D401/ 01/ 02/ 02	තැන්පත් ජනපදය ගෙදර මාර්ගය	157133.609/ 149725.826	157137.132/ 149726.868	157065.731/ 149589.514	157069.925/ 149590.522	159.34	3.0	2.0
364	SG/ APS/ B034/ D401/ 01/ 02/ 03	තැන්පත් ජනපදය ගෙදර මාර්ගයේ පළමු පටුම	157030.221/ 149714.53	157027.327/ 149713.727	156910.603/ 149791.995	156908.828/ 149789.577	189.46	3.0	3.0
365	SG/ APS/ B034/ D401/ 01/ 03	පළමු පිටකන්ද ගම්පහ පළමු මාර්ගය	157326.54/ 149849.629	157323.621/ 149852.496	157404.109/ 149821.606	157407.586/ 149823.594	114.46	4.0	3.0
366	SG/ APS/ B034/ D401/ 01/ 04	පළමු පිටකන්ද ගම්පහ දෙවන මාර්ගය	157324.255/ 149782.296	157324.224/ 149785.299	157456.781/ 149792.983	157456.728/ 149795.982	155.48	3.0	3.0
367	SG/ APS/ B034/ D401/ 01/ 05	බුබුළුගේ මාර්ගය	157310.794/ 149645.707	157312.533/ 149648.173	157543.494/ 149446.695	157542.715/ 149449.591	352.37	3.0	2.0
368	SG/ APS/ B034/ D401/ 01/ 06	පළමු ගෙදර ගම්පහ මාර්ගය	157154.466/ 149534.557	157151.607/ 149533.449	156816.662/ 149478.874	156818.62/ 149481.149	472.18	3.0	2.0


අනු. අංකය	පාරෙහි නෝනය	පාරේ නම	ආරම්භක බණ්ඩංක (කළුපිටි ලංකා)		අවසාන බණ්ඩංක (කළුපිටි ලංකා)		පාරේ දිග (මීටර්)	පාරේ සාමාන්‍ය පළල (මීටර්)	සංවර්ධිත පළල (මීටර්)
			වම	දකුණ	වම	දකුණ			
369	SG/ APS/ B034/ D401/ 01/ 07	කළුතර එළවැල්ලහේන මාර්ගය	156822.356/ 149378.184	156821.703/ 149375.114	156698.037/ 149406.824	156696.315/ 149404.368	132.69	3.0	3.0
370	SG/ APS/ B034/ D401/ 01/ 08	ලඹුගල ගෙදර මාර්ගයේ පළමු පටුම	156811.451/ 149337.844	156811.69/ 149334.842	156763.994/ 149303.041	156765.413/ 149300.397	63.81	3.0	3.0
371	SG/ APS/ B034/ D401/ 01/ 09	ගෙදර පරණ ගම්සභා මාර්ගය	156684.691/ 148304.064	156681.118/ 148302.226	156549.574/ 148301.897	156552.931/ 148304.161	182.36	4.0	4.0
372	SG/ APS/ B034/ D401/ 01/ 10	ගෙදර ආරණ්‍ය මාර්ගය	156663.245/ 147217.589	156663.011/ 147221.128	156856.926/ 147066.015	156858.919/ 147068.892	256.08	3.5	3.0
373	SG/ APS/ B034/ D401/ 01/ 11	ගෙදර හතළිහවැන්න මාර්ගය	156531.734/ 147168.814	156534.705/ 147170.276	156588.076/ 146855.55	156590.973/ 146856.33	350.74	3.0	2.5
374	SG/ APS/ B034/ D401/ 01/ 12	ගෙදර මිල්ලහේන අඩි පාර	156514.649/ 147164.072	156512.859/ 147162.653	156399.529/ 147315.415	156397.529/ 147315.453	267.89	2.0	1.0
375	SG/ APS/ B034/ D401/ 01/ 13	ගෙදර මිල්ලහේන මාර්ගය	156465.693/ 147104.555	156464.318/ 147100.354	155868.854/ 147300.375	155871.845/ 147303.031	1164.3	4.0	3.0
376	SG/ APS/ B034/ D401/ 01/ 13/ 01	ගෙදර මිල්ලහේන මාර්ගයේ පළමු පටුම	155798.488/ 147446.75	155800.358/ 147442.241	155757.427/ 147412.9	155760.911/ 147413.242	106.04	3.5	2.5
377	SG/ APS/ B034/ D401/ 01/ 14	භුල්කිරිදොළ බලාගාරය මාර්ගය	156317.778/ 146714.349	156320.348/ 146716.86	157384.536/ 146089.61	157388.032/ 146089.765	1505.7	3.5	2.5


අනු-අංකය	පාරමිති කේතය	පාරමිති නම	ආරම්භක බණ්ඩාංක (කදවල ශ්‍රී ලංකා)		අවසාන බණ්ඩාංක (කදවල ශ්‍රී ලංකා)		පාරමිති දිග (මීටර්)	පාරමිති පළල (මීටර්)	සංවර්ධන පළල (මීටර්)
			වම	දකුණ	වම	දකුණ			
378	SG/ APS/ B034/ D401/ 02	උඩුගල අඟුරුවෙල මාර්ගයේ පළමු පටුම	157148.367/ 150420.874	157150.959/ 150419.323	156956.706/ 150276.248	156955.504/ 150273.499	276.08	3.0	3.0
379	SG/ APS/ B034/ D401/ 02/ 01	ශ්‍රී ධර්මරක්ෂිතාමය මාර්ගය	157080.52/ 150372.702	157078.667/ 150369.666	157022.099/ 150382.247	157020.6/ 150379.648	61.74	3.0	3.0
380	SG/ APS/ B034/ D401/ 03	උඩුගල අඟුරුවෙල මාර්ගයේ දෙවන පටුම	156827.768/ 150588.171	156824.818/ 150587.482	156791.117/ 150679.513	156788.524/ 150678.006	102.04	3.0	3.0
381	SG/ APS/ B034/ D401/ 04	අඟුරුවෙල පරික්ෂිත පළමු මාර්ගය	156693.755/ 150550.761	156696.529/ 150551.993	156751.097/ 150216.214	156753.191/ 150218.367	546.79	3.0	2.5
382	SG/ APS/ B034/ D401/ 05	උඩුගල අඟුරුවෙල මාර්ගයේ තෙවන පටුම	156584.485/ 150624.643	156582.288/ 150627.259	156643.239/ 150734.101	156640.736/ 150732.446	153.86	3.0	2.5
383	SG/ APS/ B034/ D401/ 06	හඳුන්කන්ද බටහේන මාර්ගය	156040.438/ 150792.897	156036.998/ 150795.111	156122.938/ 150988.518	156122.743/ 150992.513	327.12	4.0	2.6
384	SG/ APS/ B034/ D401/ 06/ 01	හඳුන්කන්ද බටහේන මාර්ගයේ පළමු පටුම	156062.901/ 151020.222	156058.403/ 151020.36	156121.892/ 151137.242	156119.409/ 151140.995	157.53	4.5	2.0
385	SG/ APS/ B034/ D401/ 07	හඳුන්කන්ද පාසල් මාර්ගය	155993.968/ 150808.67	155990.983/ 150808.333	155932.163/ 150913.026	155929.876/ 150914.969	152.82	3.0	2.0
386	SG/ APS/ B034/ D401/ 08	හඳුන්කන්ද පළමු පටුම	155941.04/ 150567.698	155942.719/ 150571.068	156052.536/ 150397.226	156055.058/ 150399.652	219.62	3.5	2.5
387	SG/ APS/ B034/ D401/ 09	අඟුරුවෙල පරික්ෂිත දෙවන මාර්ගය	155416.689/ 150299.172	155423.355/ 150297.887	156700.848/ 150198.96	156696.86/ 150194.851	2147.1	4.0	2.5
388	SG/ APS/ B034/ D401/ 10	උඩුගල අඟුරුවෙල මාර්ගයේ සිව්වන පටුම	155255.126/ 150278.066	155258.442/ 150279.193	155301.796/ 150099.024	155303.867/ 150101.844	238.52	3.5	3.0


අනු. අංකය	පාරමිති කේතය	පාරමිති නම	ආරම්භක බණ්ඩංගු (කළුපිටි ලියවීම)		අවසාන බණ්ඩංගු (කළුපිටි ලියවීම)		පාරමිති දිග (මීටර්)	පාරමිති පළල (මීටර්)	සංවර්ධන පළල (මීටර්)
			වම	දකුණ	වම	දකුණ			
389	SG/ APS/ B034/ D401/ 11	අඟුරුවෙල වැනිය අඩි පාර	154924.975/ 150380.579	154922.681/ 150383.016	154917.22/ 151066.195	154917.112/ 151069.193	975.28	3.0	2.0
390	SG/ APS/ B034/ D401/ 12	පන්විලහේන පළමු පටුම	154663.695/ 150905.562	154663.531/ 150901.319	154547.724/ 151089.588	154544.204/ 151091.487	247.05	4.0	3.0
391	SG/ APS/ B034/ D401/ 13	අඟුරුවෙල පන්විලහේන මාර්ගය	154671.092/ 150934.792	154668.105/ 150935.088	154379.255/ 151278.751	154379.522/ 151275.763	586.84	3.0	3.0
392	SG/ APS/ B034/ D401/ 13/ 01	පන්විලහේන දෙවන පටුම - අඩි පාර	154643.94/ 151182.473	154640.685/ 151184.567	154534.83/ 151309.855	154534.658/ 151306.859	211.24	3.0	1.0
393	SG/ APS/ B034/ C403/ 01	වේරගමකන්ද මාර්ගය	153527.299/ 154057.44	153527.251/ 154061.441	154282.721/ 153664.727	154279.844/ 153667.505	989.79	4.0	4.0
394	SG/ APS/ B034/ C403/ 02	කුකුළුවා රජමහා විහාර පළමු මාවත	153415.092/ 154520.334	153416.359/ 154526.083	154548.876/ 155593.224	154549.724/ 155596.62	2129.06	3.5	3.0
395	SG/ APS/ B034/ C403/ 02/ 01	කරවිලහේන මාර්ගය	153688.552/ 154709.874	153688.286/ 154714.284	153796.476/ 154135.909	153799.374/ 154136.687	788.25	3.0	2.5
396	SG/ APS/ B034/ C403/ 03	වැල්ලවත්ත නාවික මාර්ගය	153491.897/ 154877.567	153490.694/ 154874.125	153259.975/ 154932.132	153257.195/ 154930.006	306.89	3.5	3.0
397	SG/ APS/ B034/ C403/ 04	කුකුළුවා රජමහා විහාර අඩි පාර	153515.858/ 154959.691	153515.612/ 154961.225	153738.21/ 155002.228	153738.768/ 155003.684	247.55	1.5	1.5


අනු. අංකය	පාරමිති කේතය	පාරමිති නම	ආරම්භක බණ්ඩාංක (කදවල ශ්‍රී ලංකා)		අවසාන බණ්ඩාංක (කදවල ශ්‍රී ලංකා)		පාරමිති දිග (මීටර්)	පාරමිති පළල (මීටර්)	සංවර්ධිත පළල (මීටර්)
			වම	දකුණ	වම	දකුණ			
398	SG/ APS/ B034/ C403/ 05	නාවිකවත්ත දේවාල මාර්ගය	153482.602/ 155076.016	153484.102/ 155072.29	153258.283/ 155086.651	153261.462/ 155085.185	312.38	3.5	3.5
399	SG/ APS/ B034/ C403/ 06	නාවිකවත්ත කුරුමා මාර්ගය	153329.396/ 155519.527	153332.445/ 155516.448	153150.443/ 155626.267	153150.56/ 155630.266	364.51	4.0	3.0
400	SG/ APS/ B034/ C403/ 06/ 01	නාවිකවත්ත මඩිත්ත මාර්ගය	153156.402/ 155509.905	153159.597/ 155508.082	152728.705/ 155356.83	152726.554/ 155354.461	1343.14	3.2	3.0
401	SG/ APS/ B034/ C403/ 07	පිඬුර කලවාන මාර්ගය	153417.591/ 155745.569	153416.569/ 155740.593	152709.9/ 156242.322	152708.631/ 156237.485	1060.64	5.0	4.0
402	SG/ APS/ B034/ C403/ 07/ 01	තැන්නේන මාර්ගය	152870.605/ 156202.46	152865.714/ 156201.659	153234.208/ 156678.36	153231.423/ 156675.489	1137.57	4.0	3.0
403	SG/ APS/ B034/ C403/ 08	කුකුළු මාර්ගය රජමහා විහාර දෙවන මාවත	153463.565/ 156000.401	153462.728/ 156003.372	154024.251/ 155442.209	154026.865/ 155440.112	864.91	3.0	3.0
404	SG/ APS/ B034/ C403/ 09	පිඬුර කරවිට මාර්ගයේ පළමු පටුම	153460.226/ 156158.501	153460.447/ 156165.711	153510.578/ 156229.595	153508.374/ 156232.314	90.02	3.5	3.0
405	SG/ APS/ B034/ C403/ 10	පිඬුර කරවිට මාර්ගයේ දෙවන පටුම	153459.349/ 156263.282	153460.227/ 156267.562	153532.008/ 156308.444	153530.977/ 156311.79	89.52	3.5	3.0
406	SG/ APS/ B421/ C428/ 01	කුකුළු මාර්ගය ජාතික මාර්ගය	153463.408/ 150016.386	153462.085/ 150021.274	154167.955/ 149520.647	154171.478/ 149517.099	979.21	5.0	3.0
407	SG/ APS/ B421/ C428/ 02	නිදන්ගල පන්සල මාර්ගය	153121.918/ 149082.771	153121.754/ 149078.768	152640.684/ 149889.154	152636.832/ 149890.232	1216.06	4.0	2.5

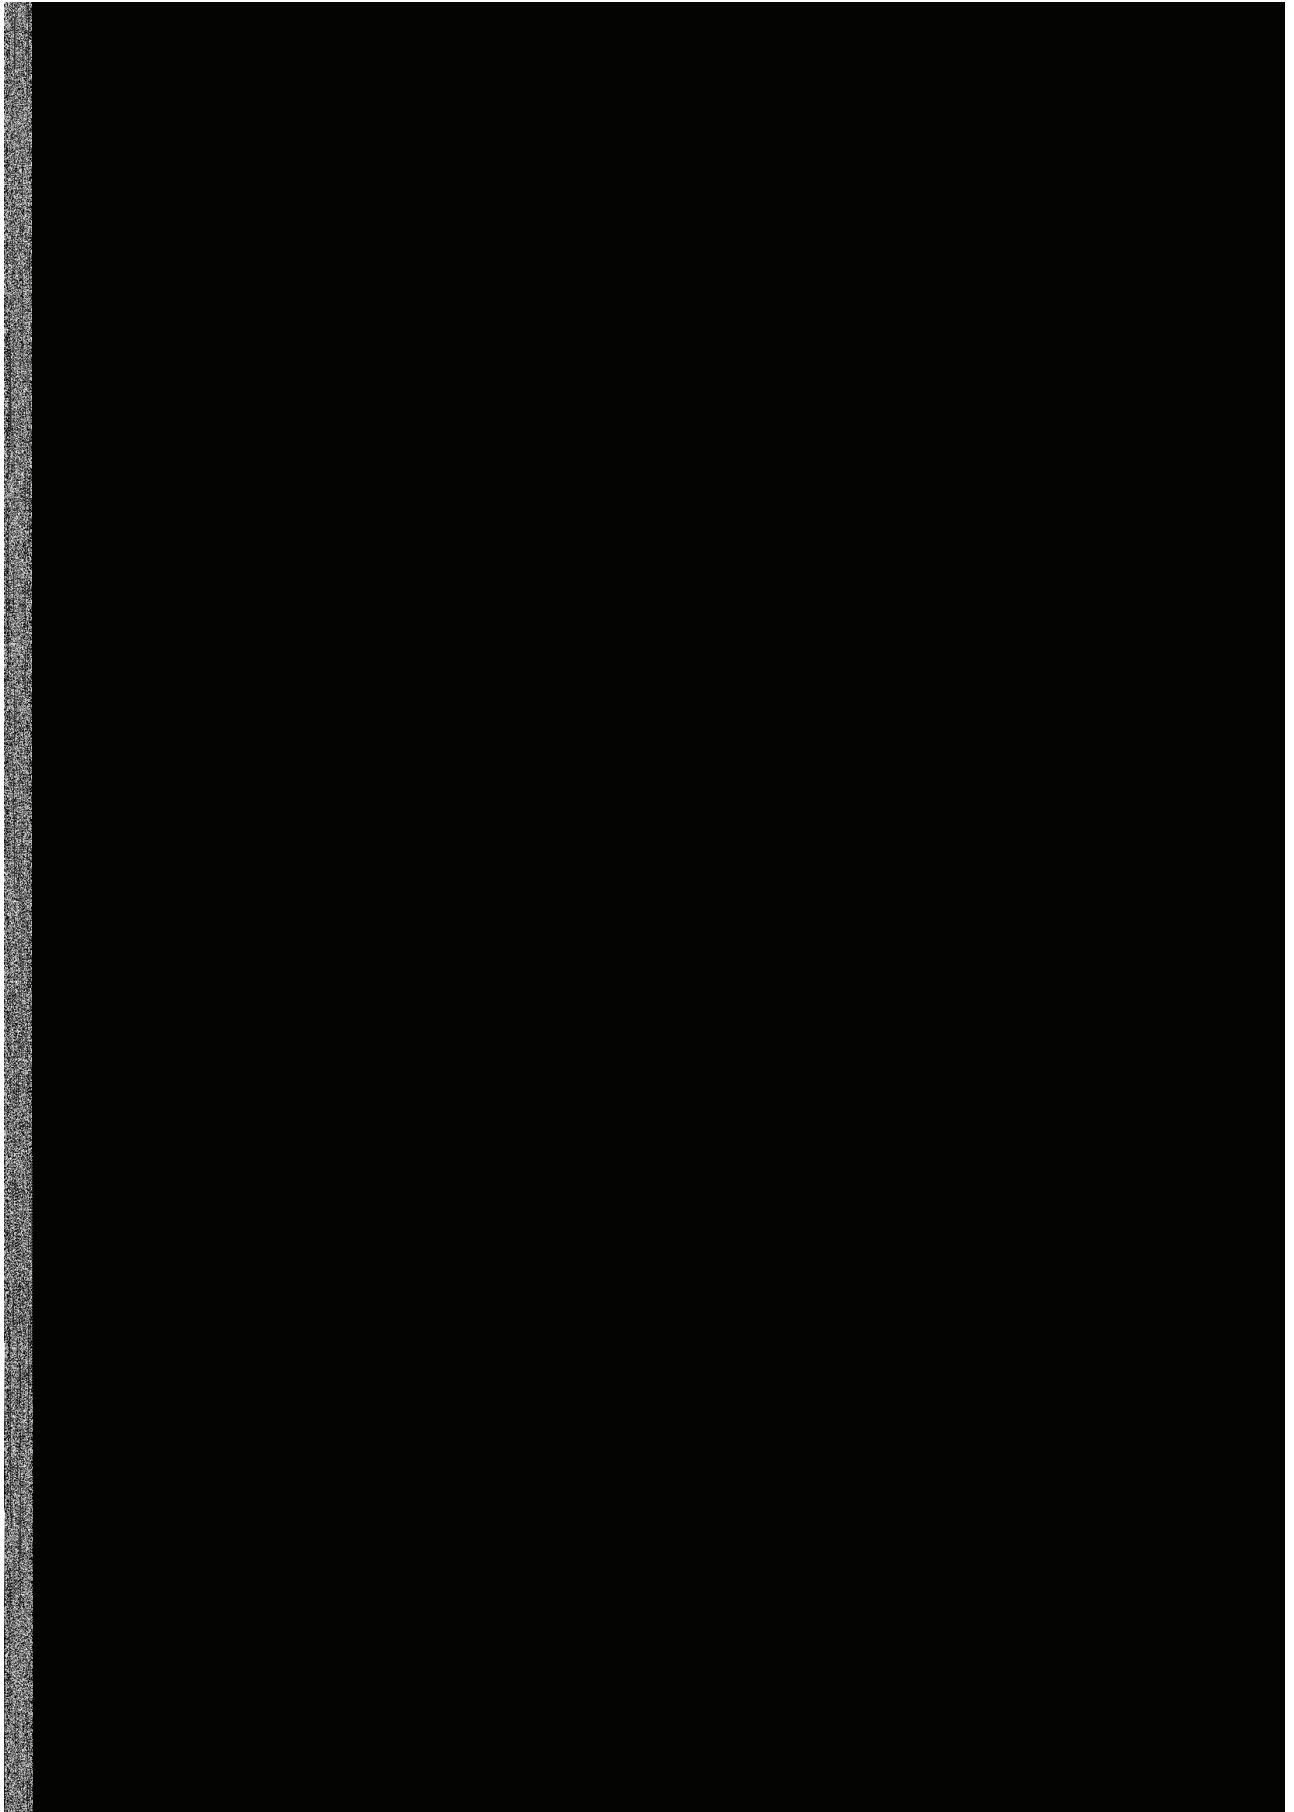


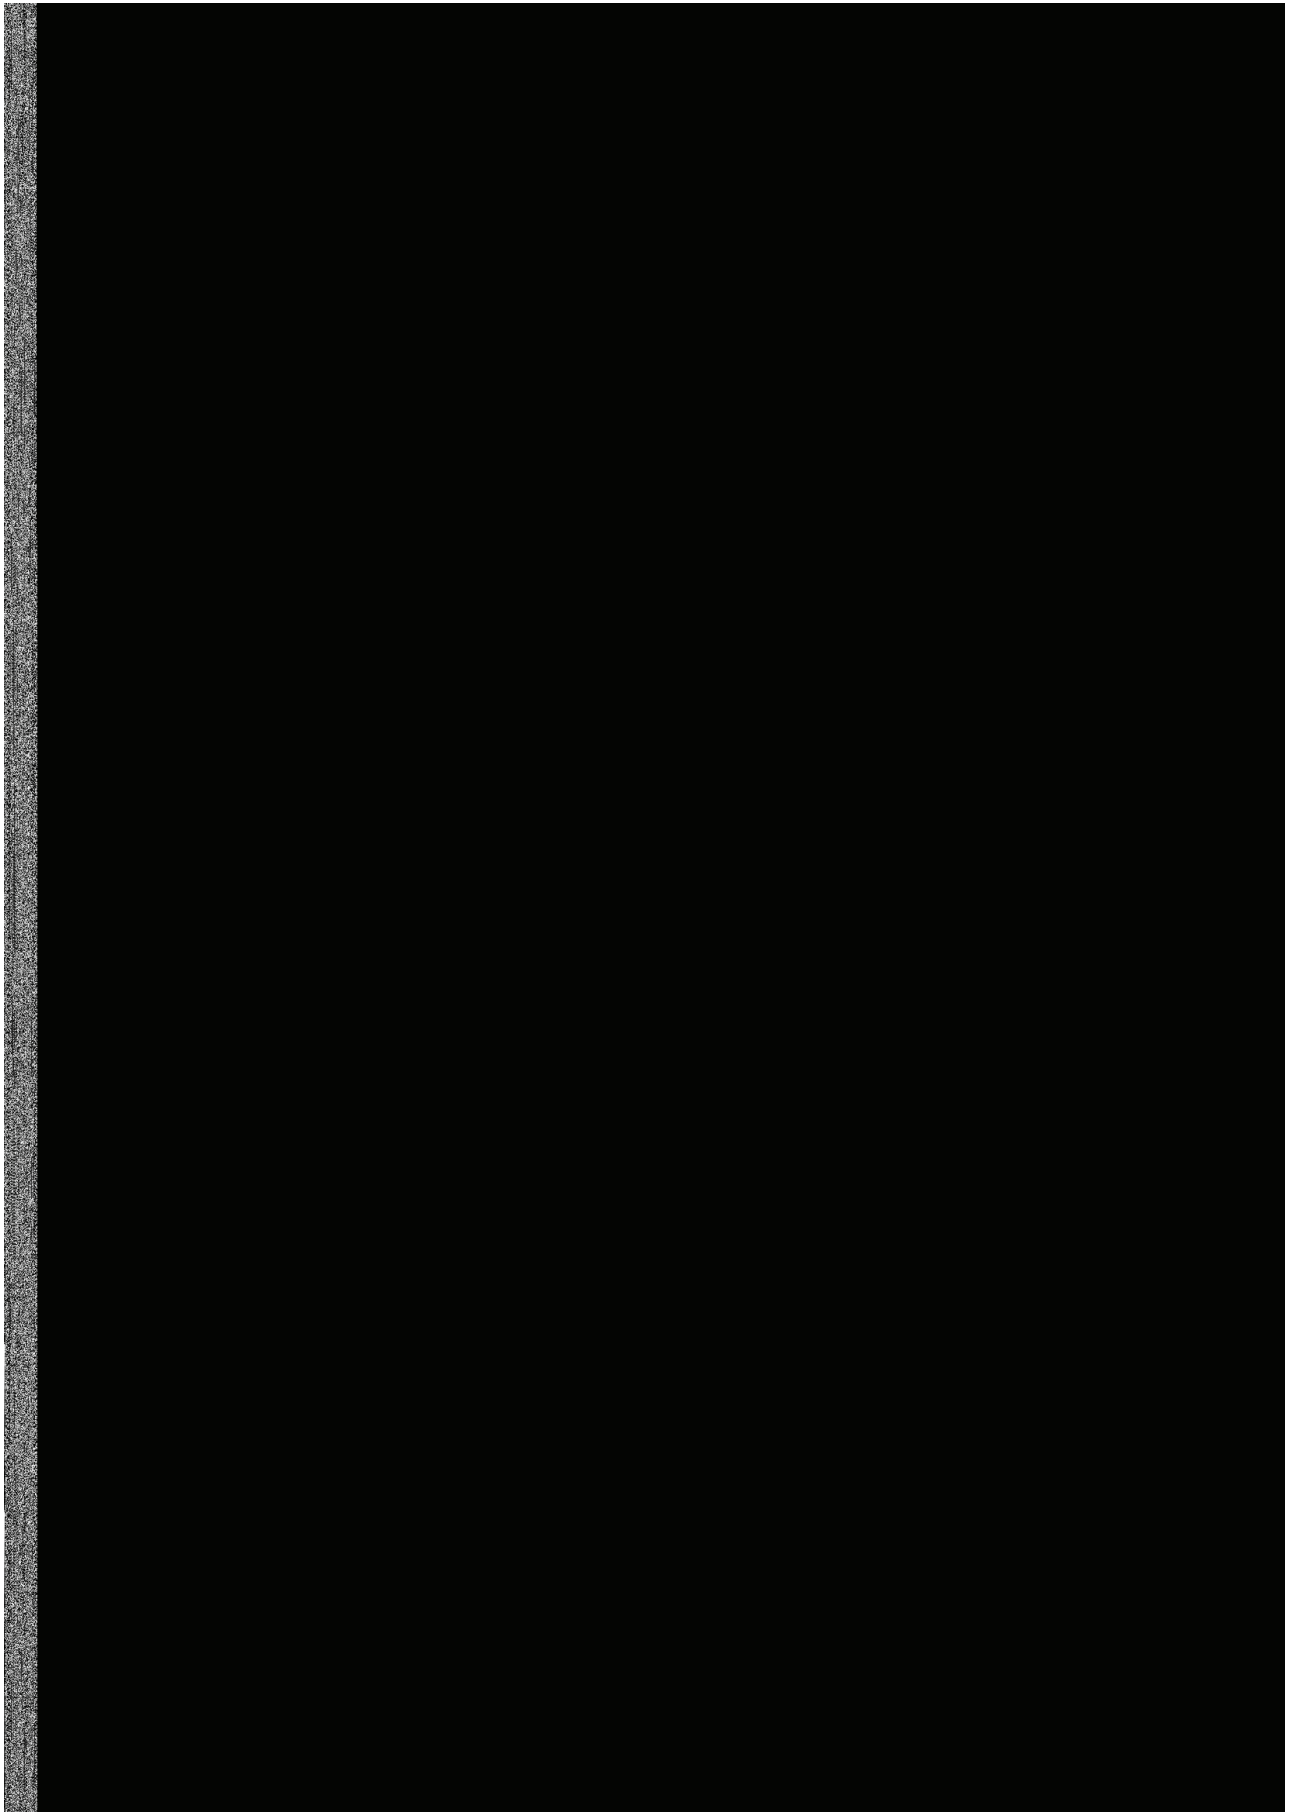


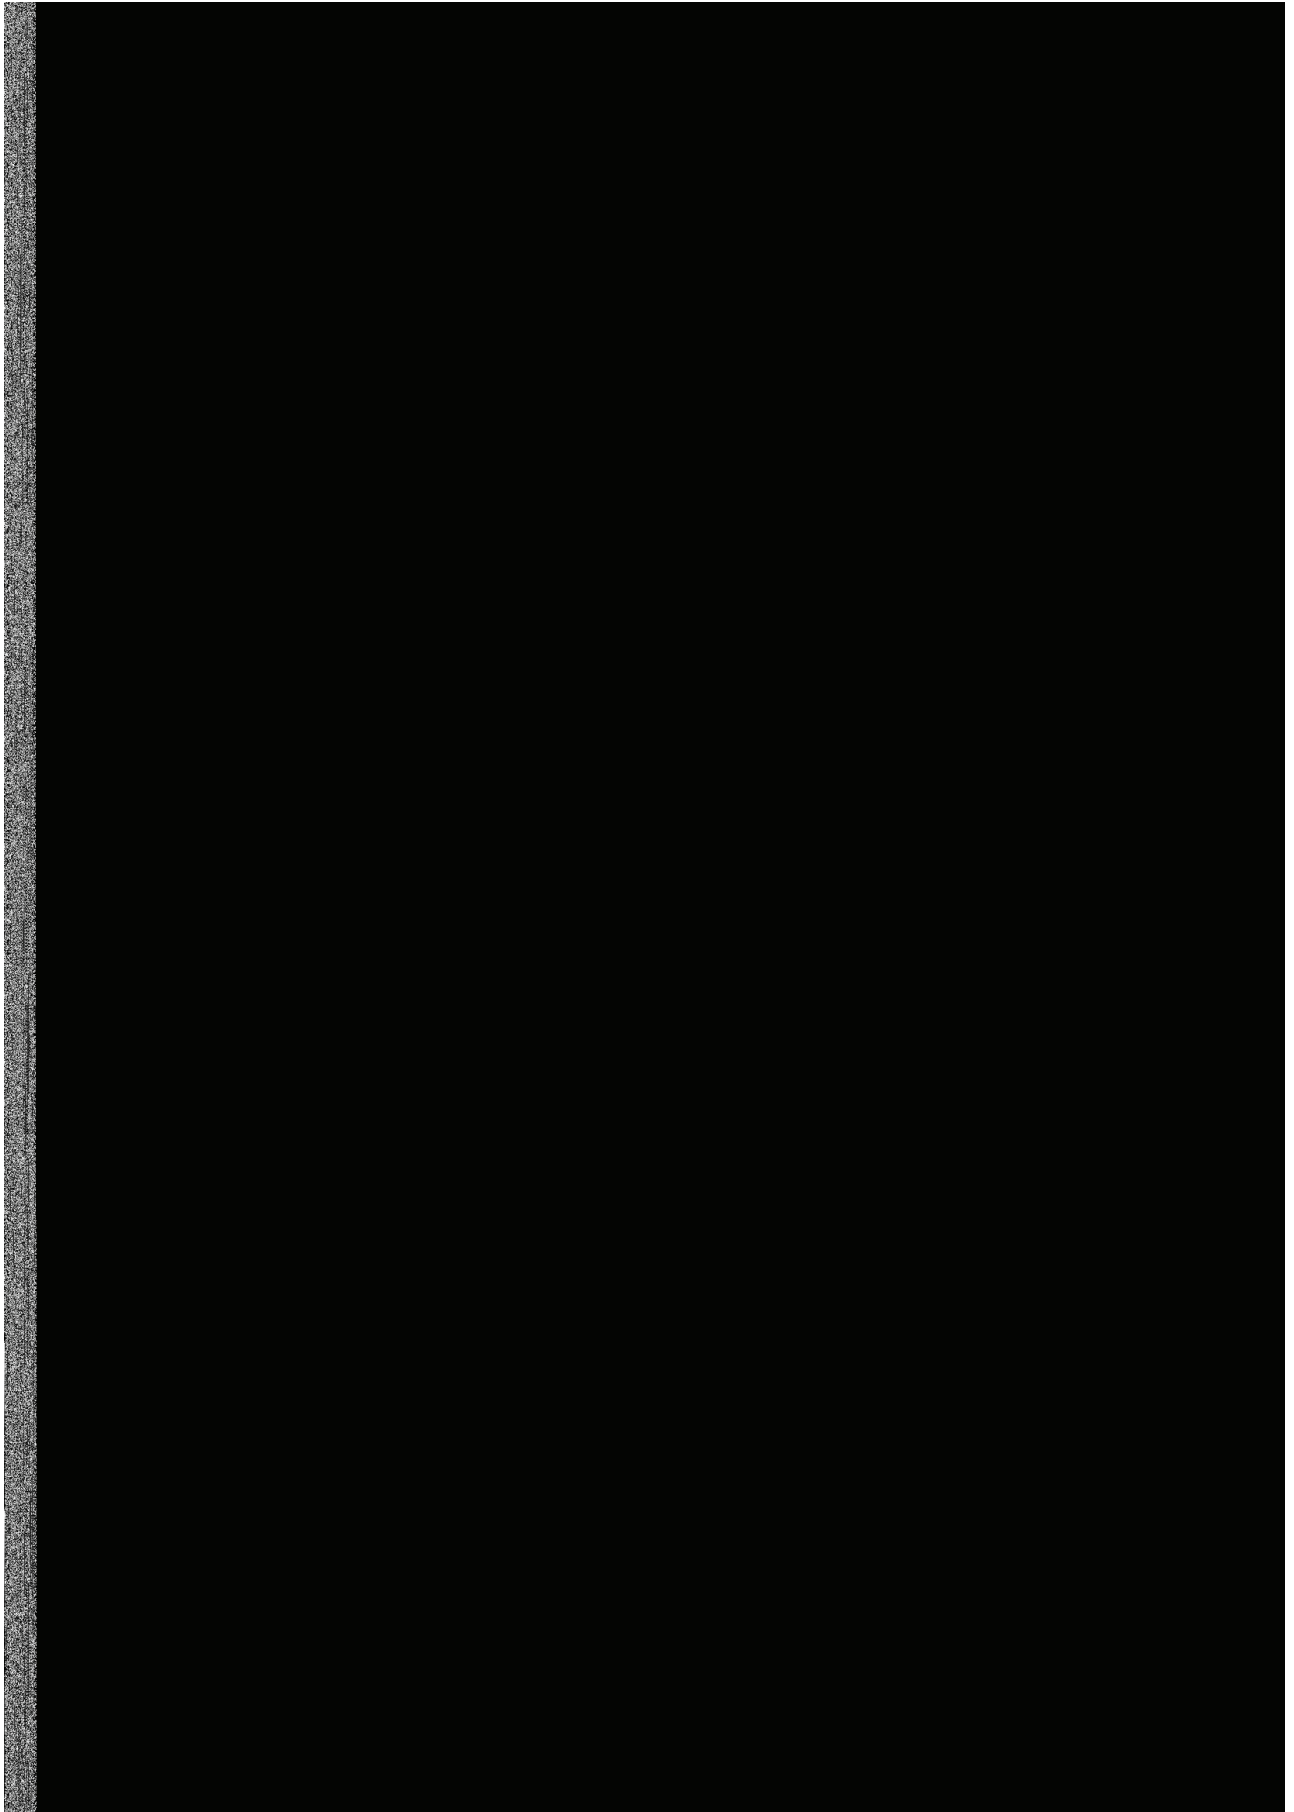


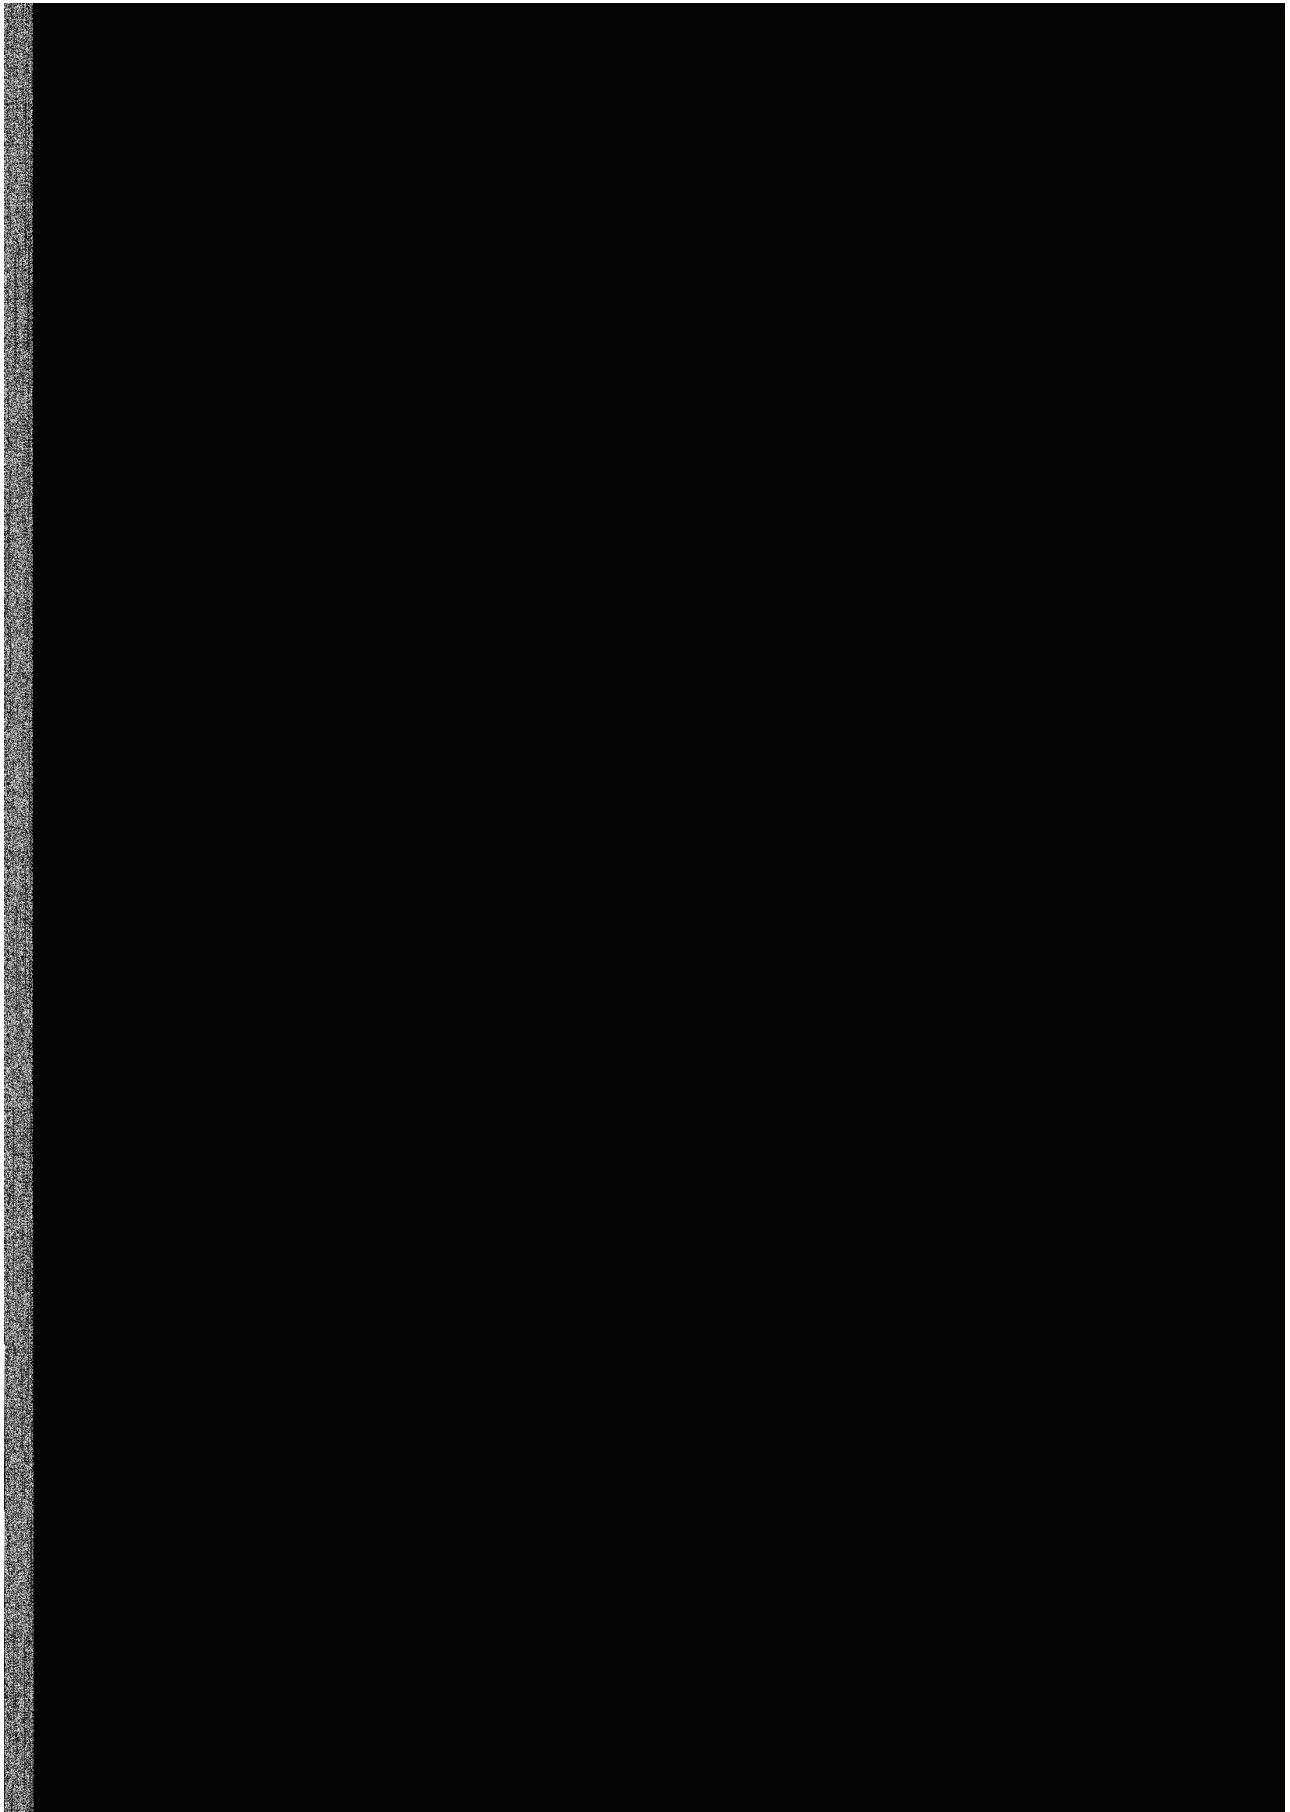


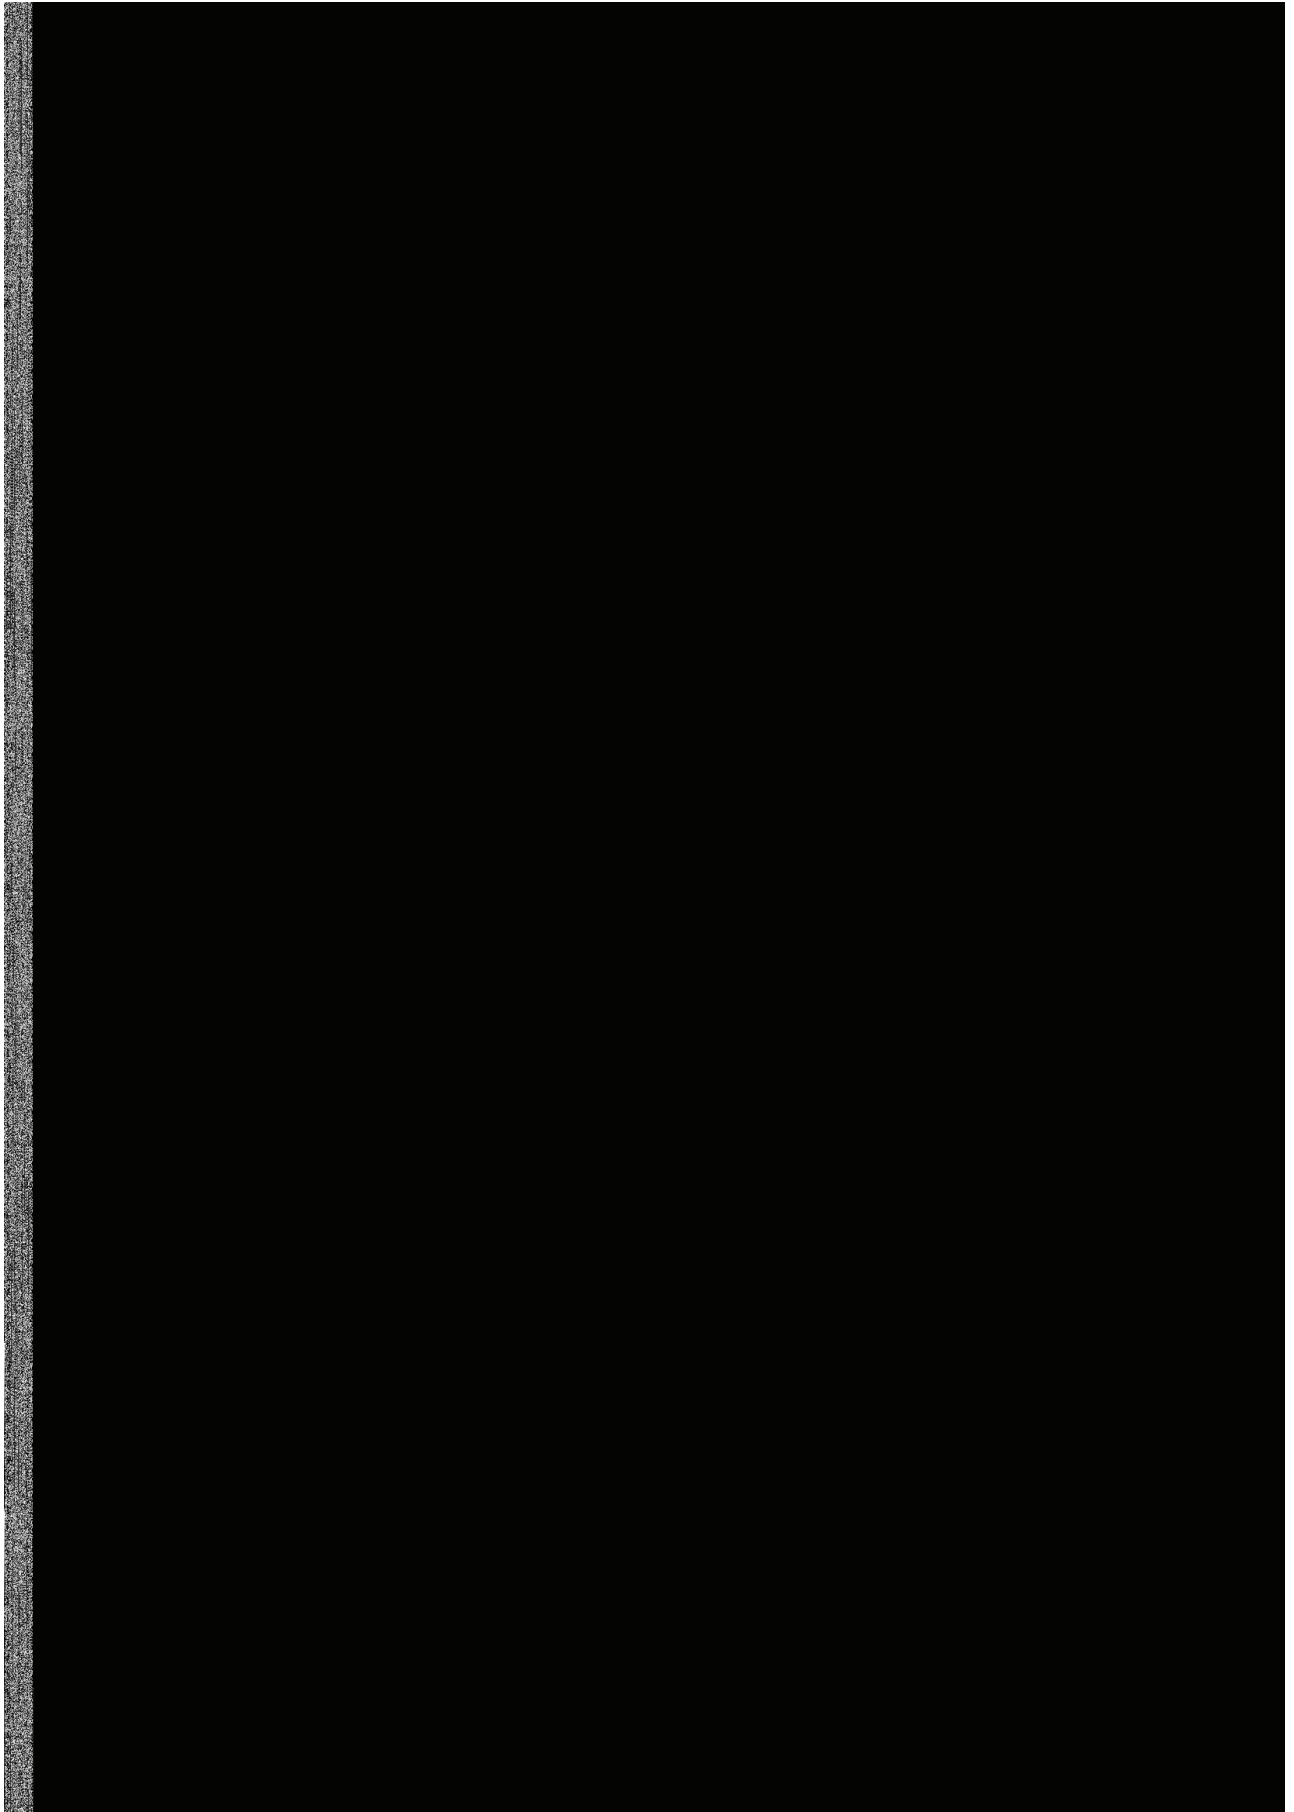


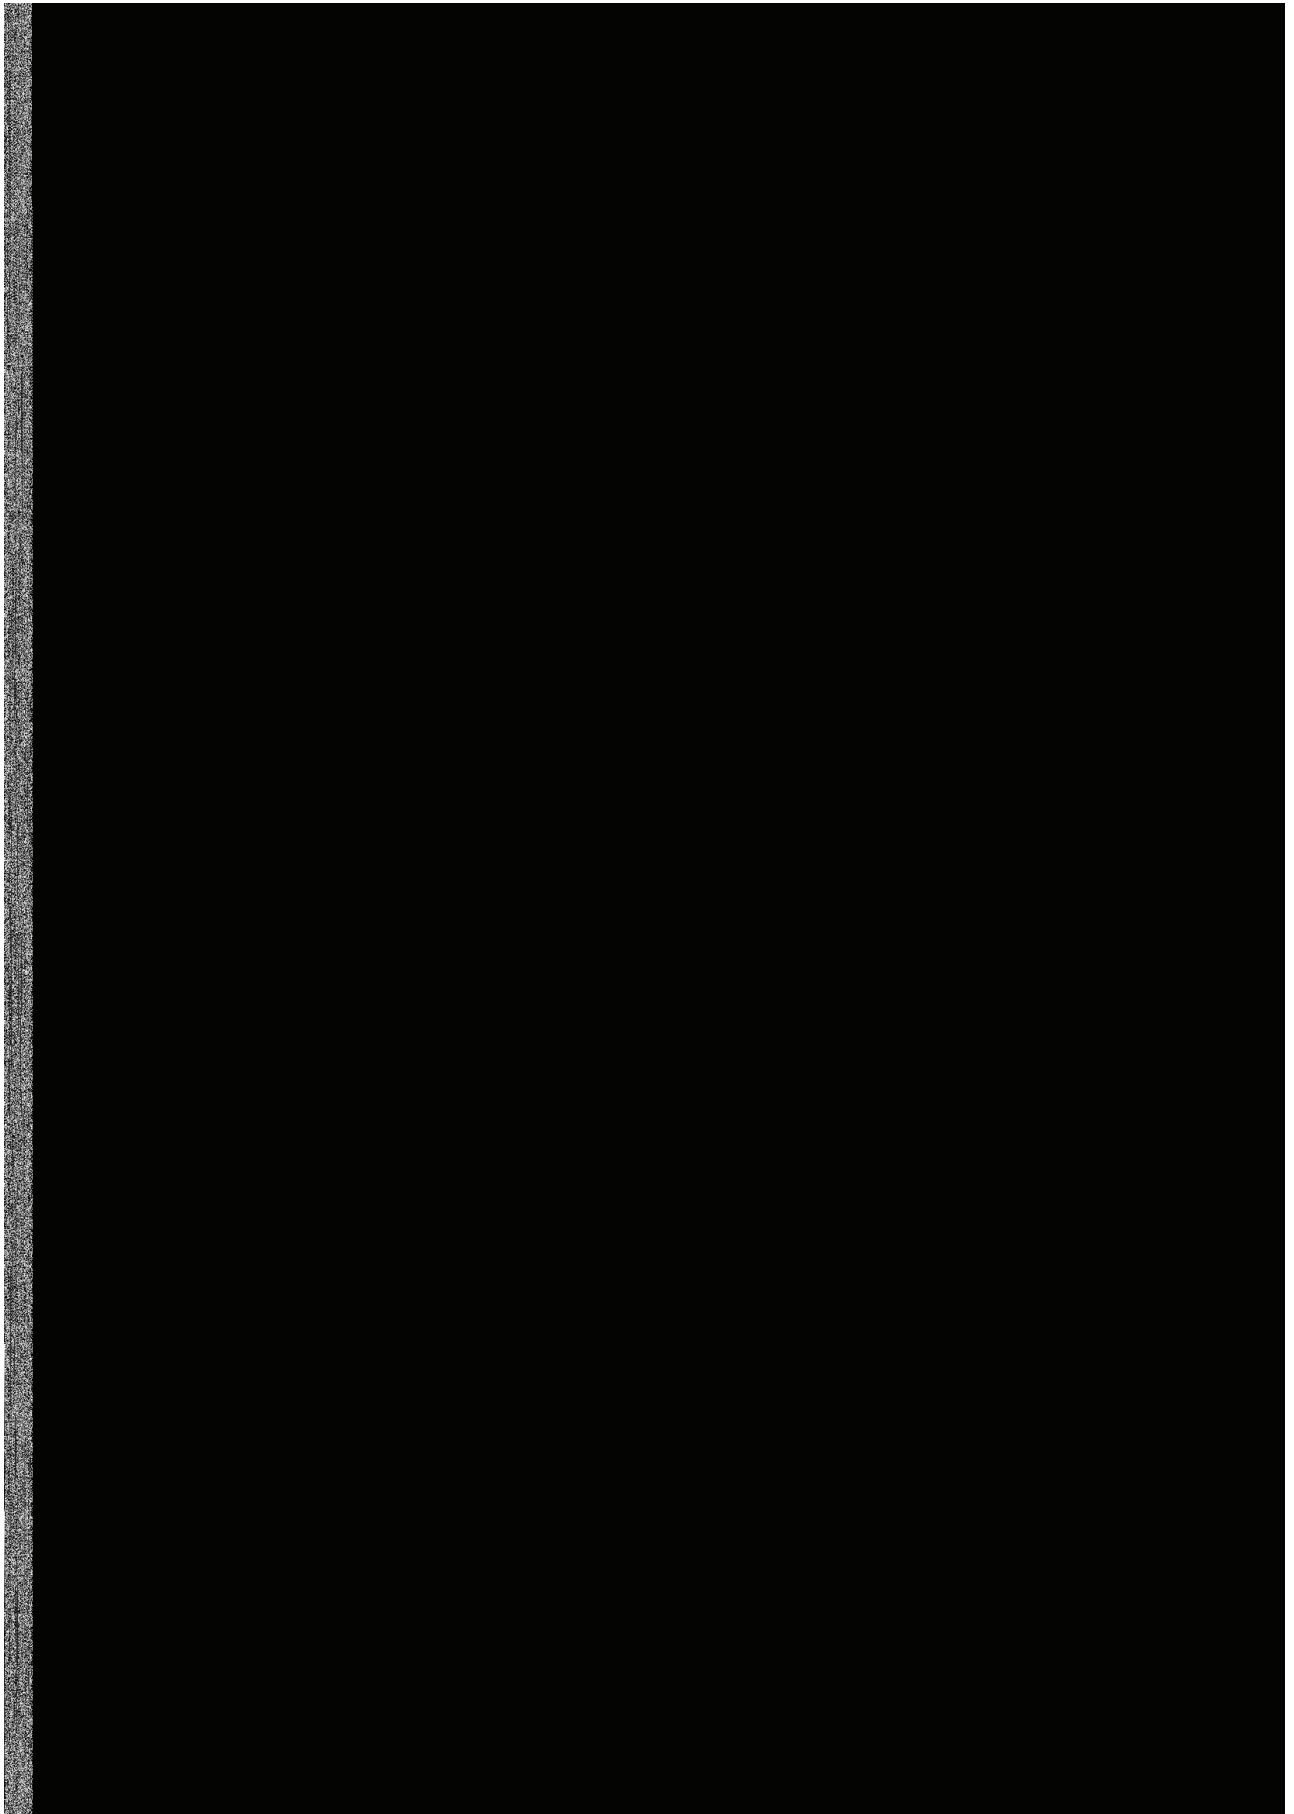


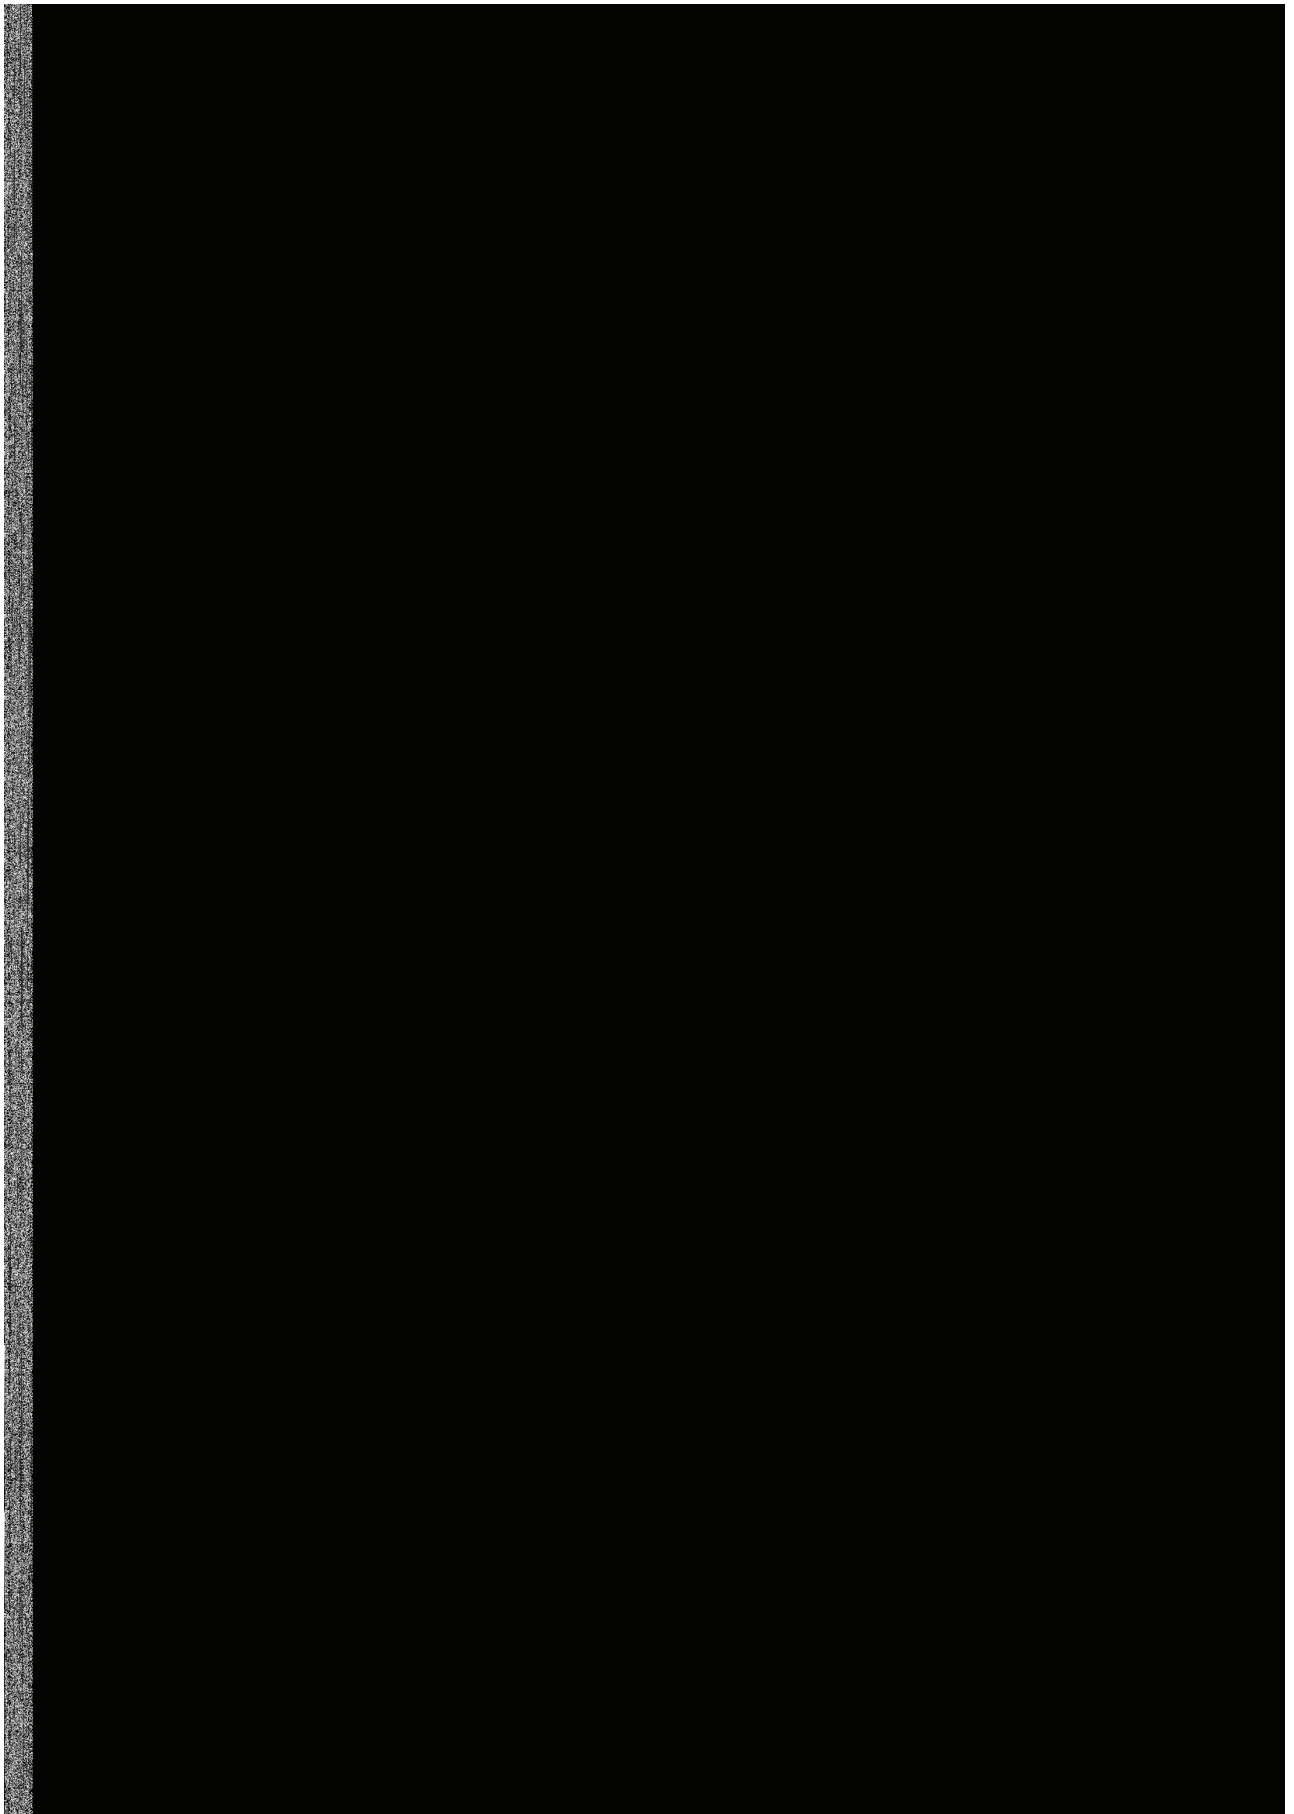


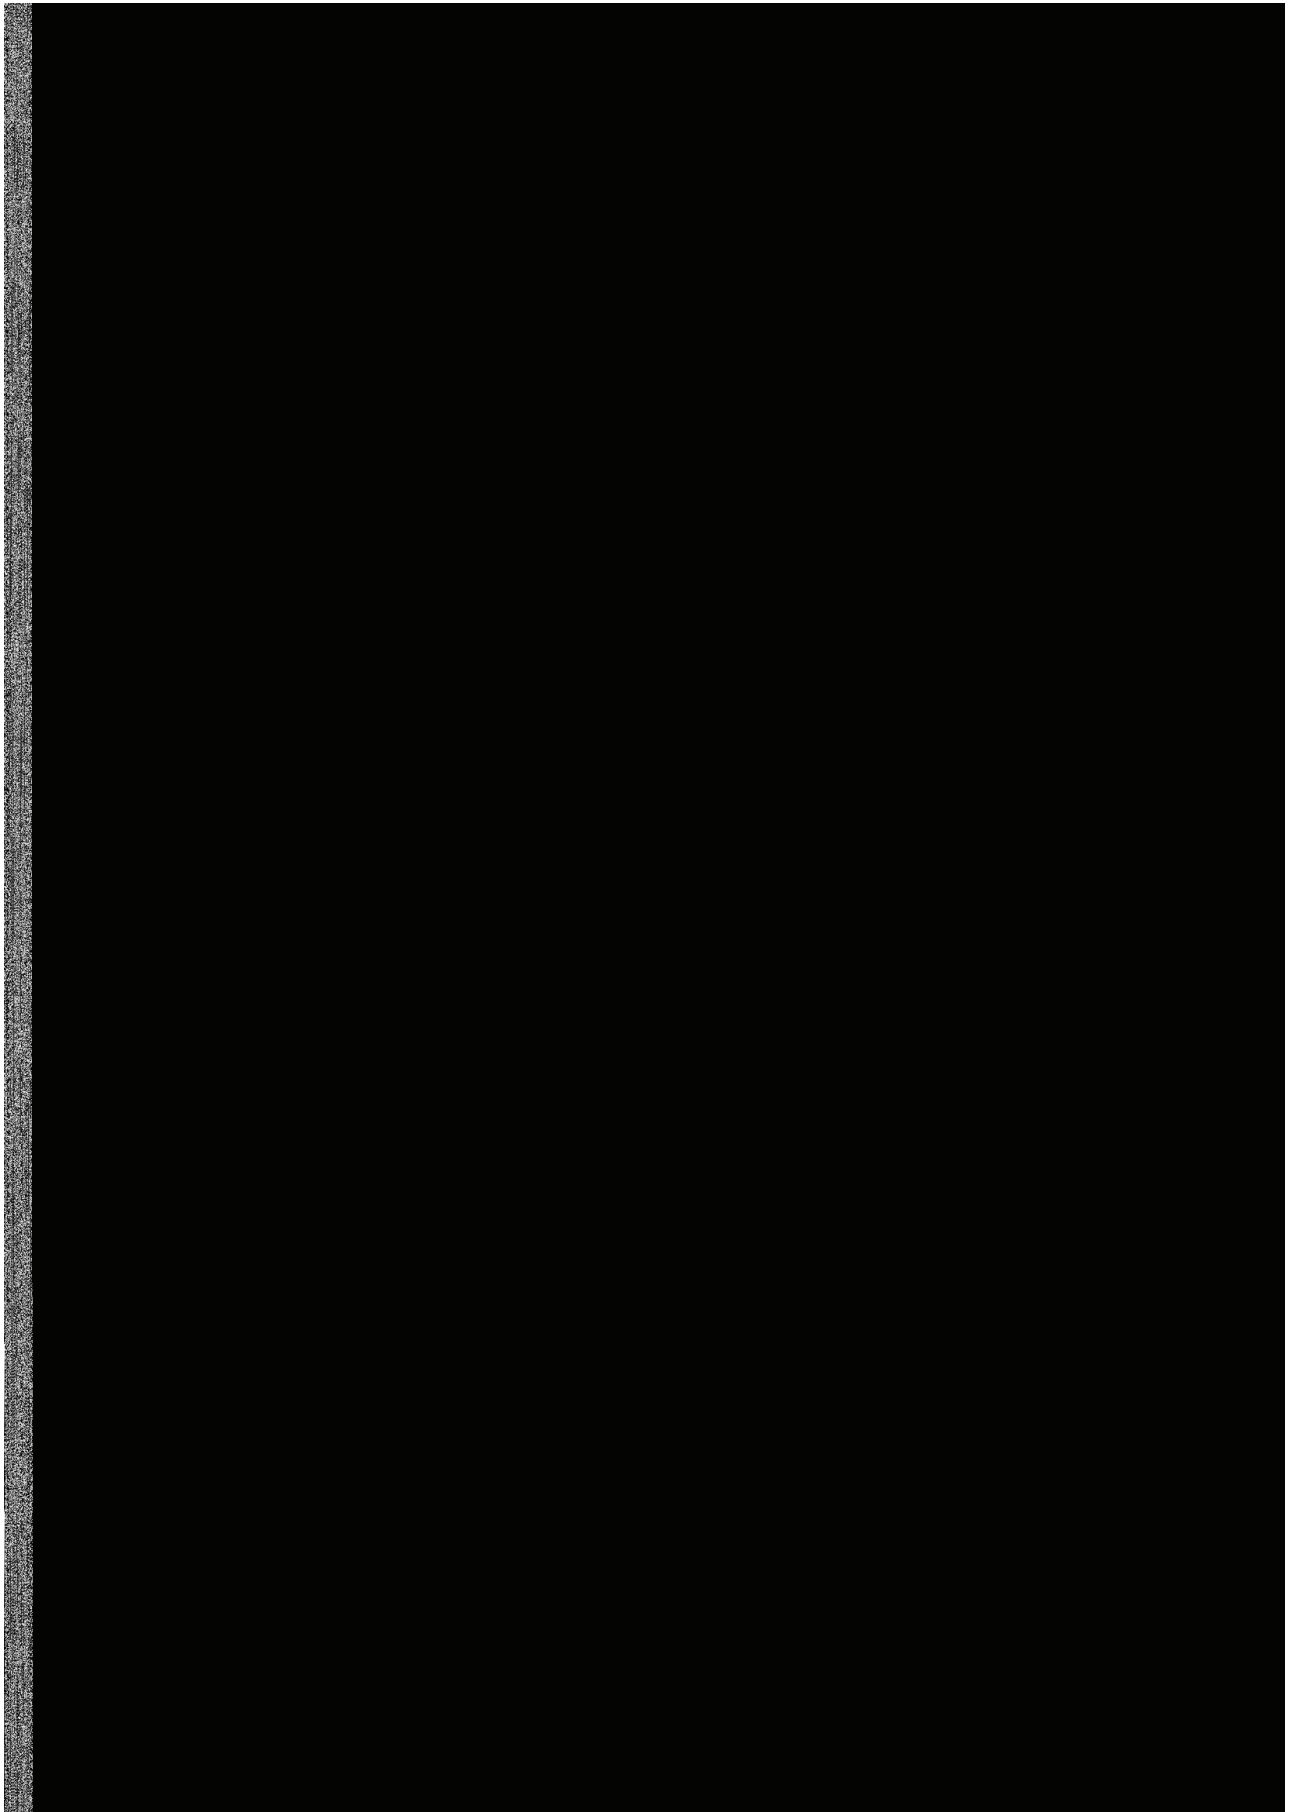

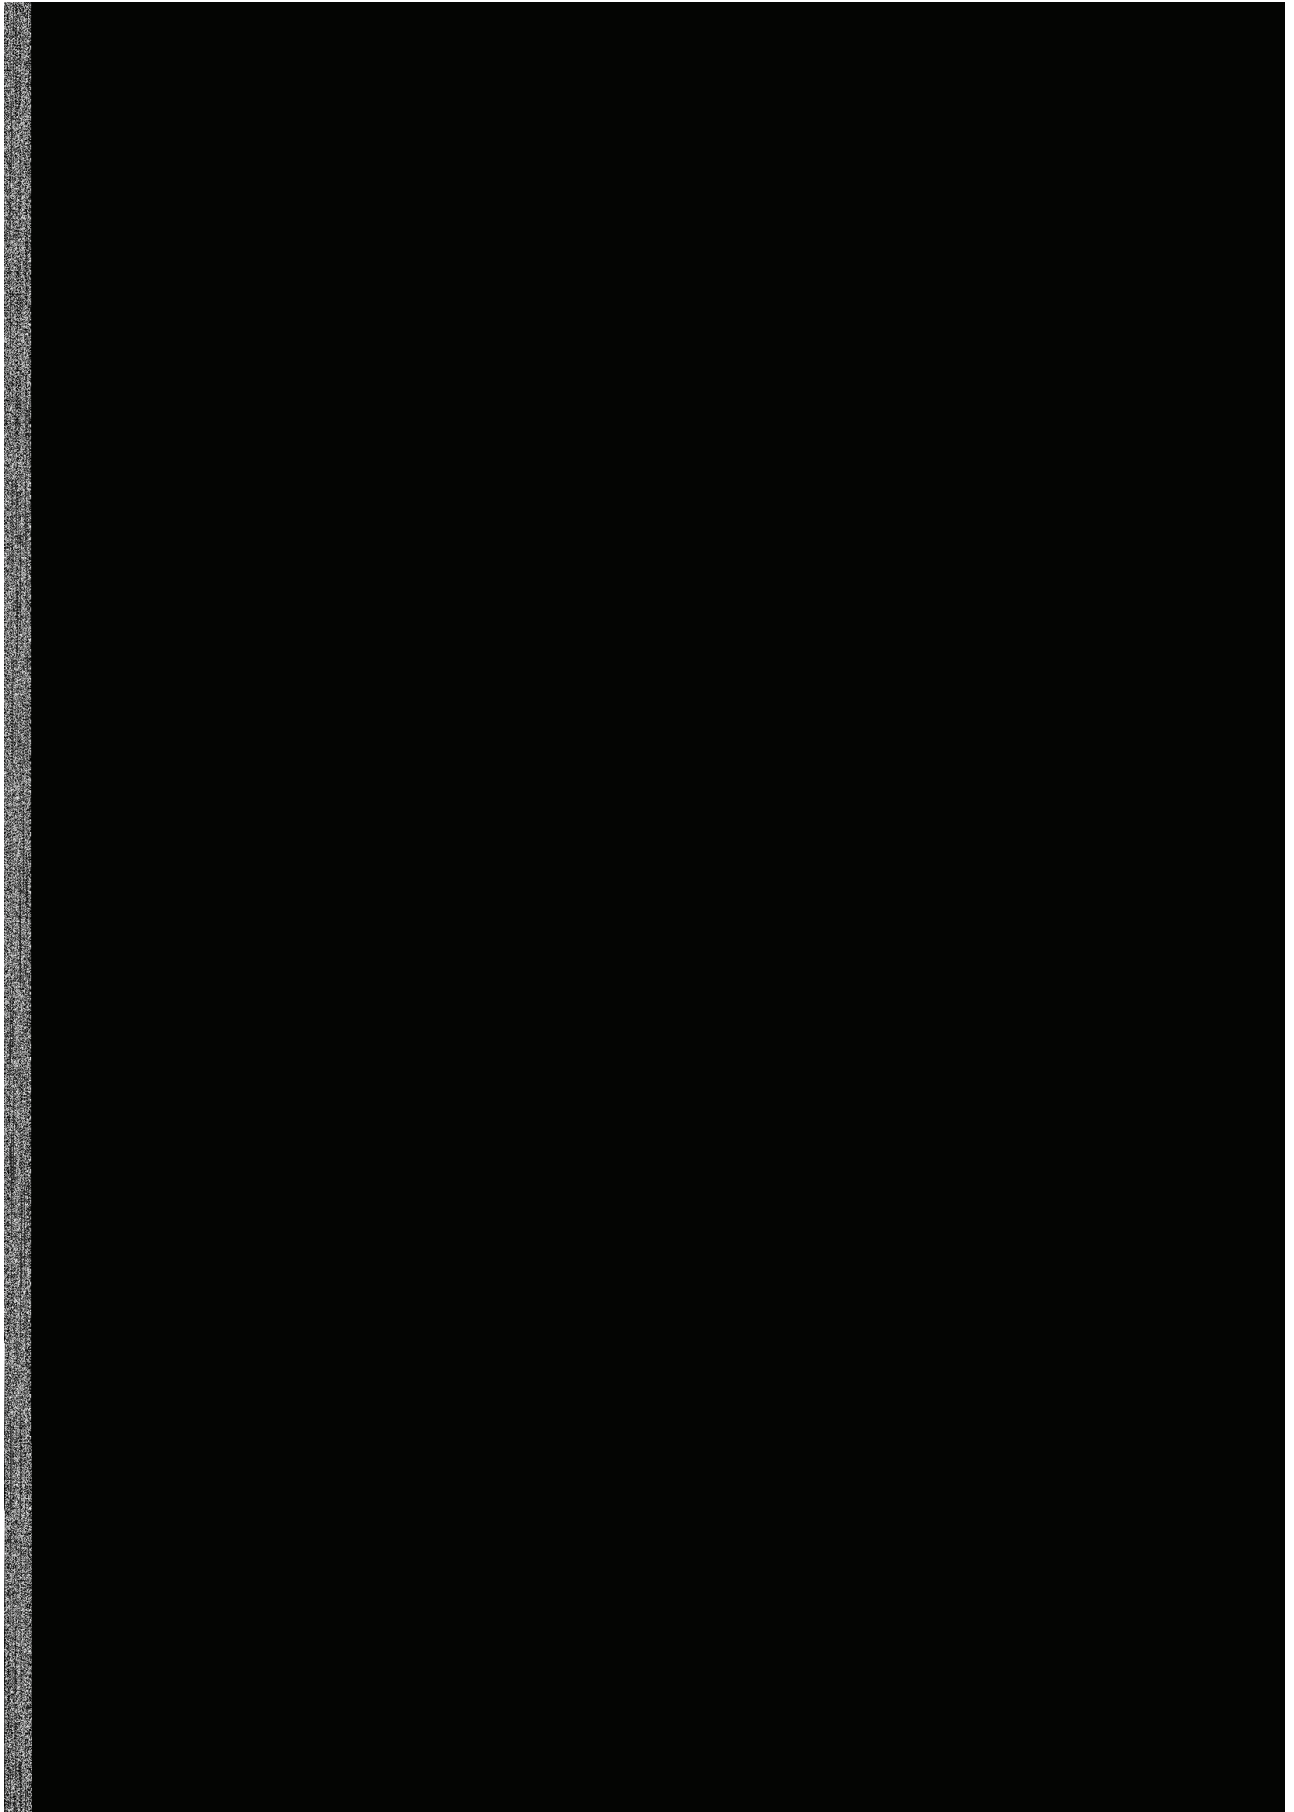


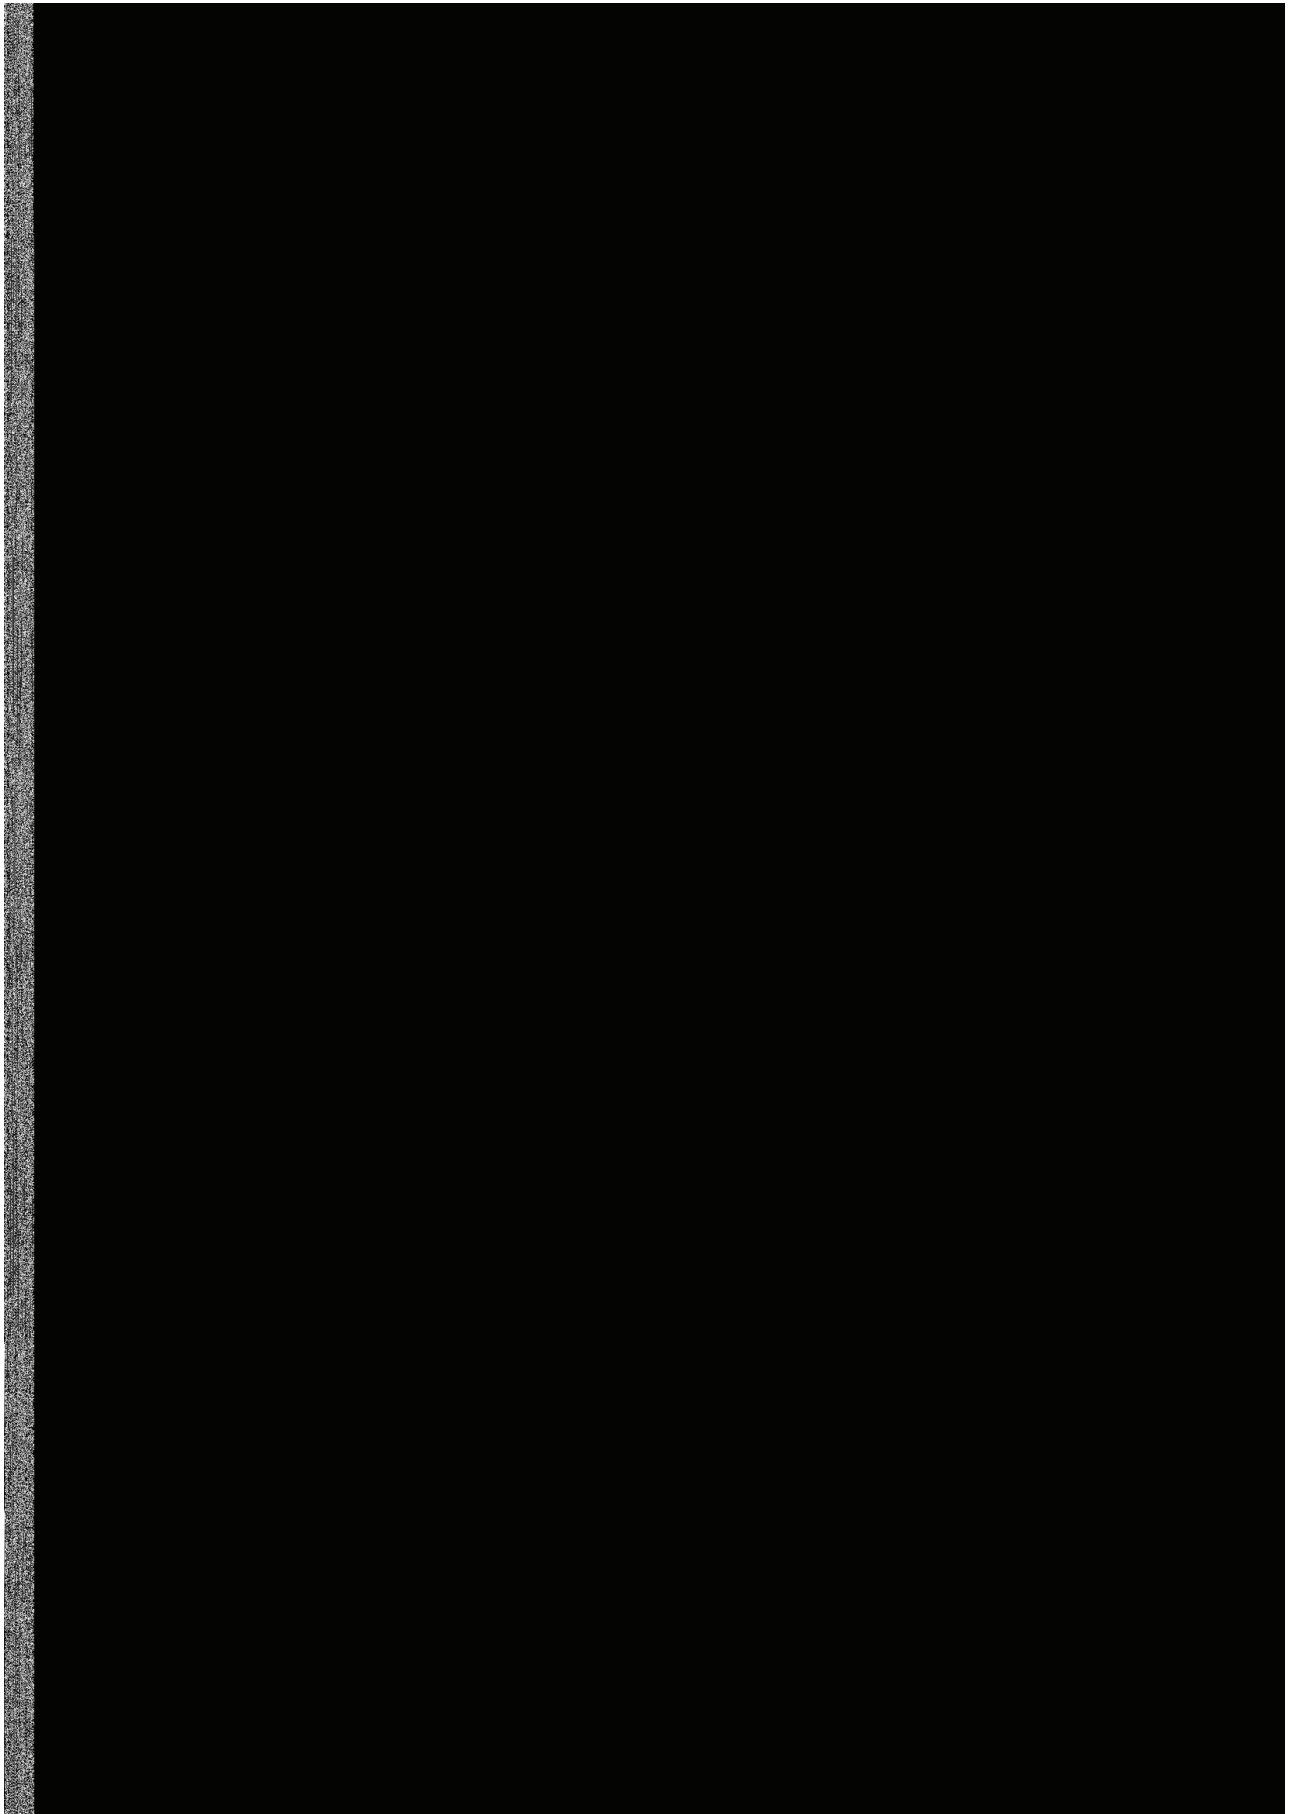


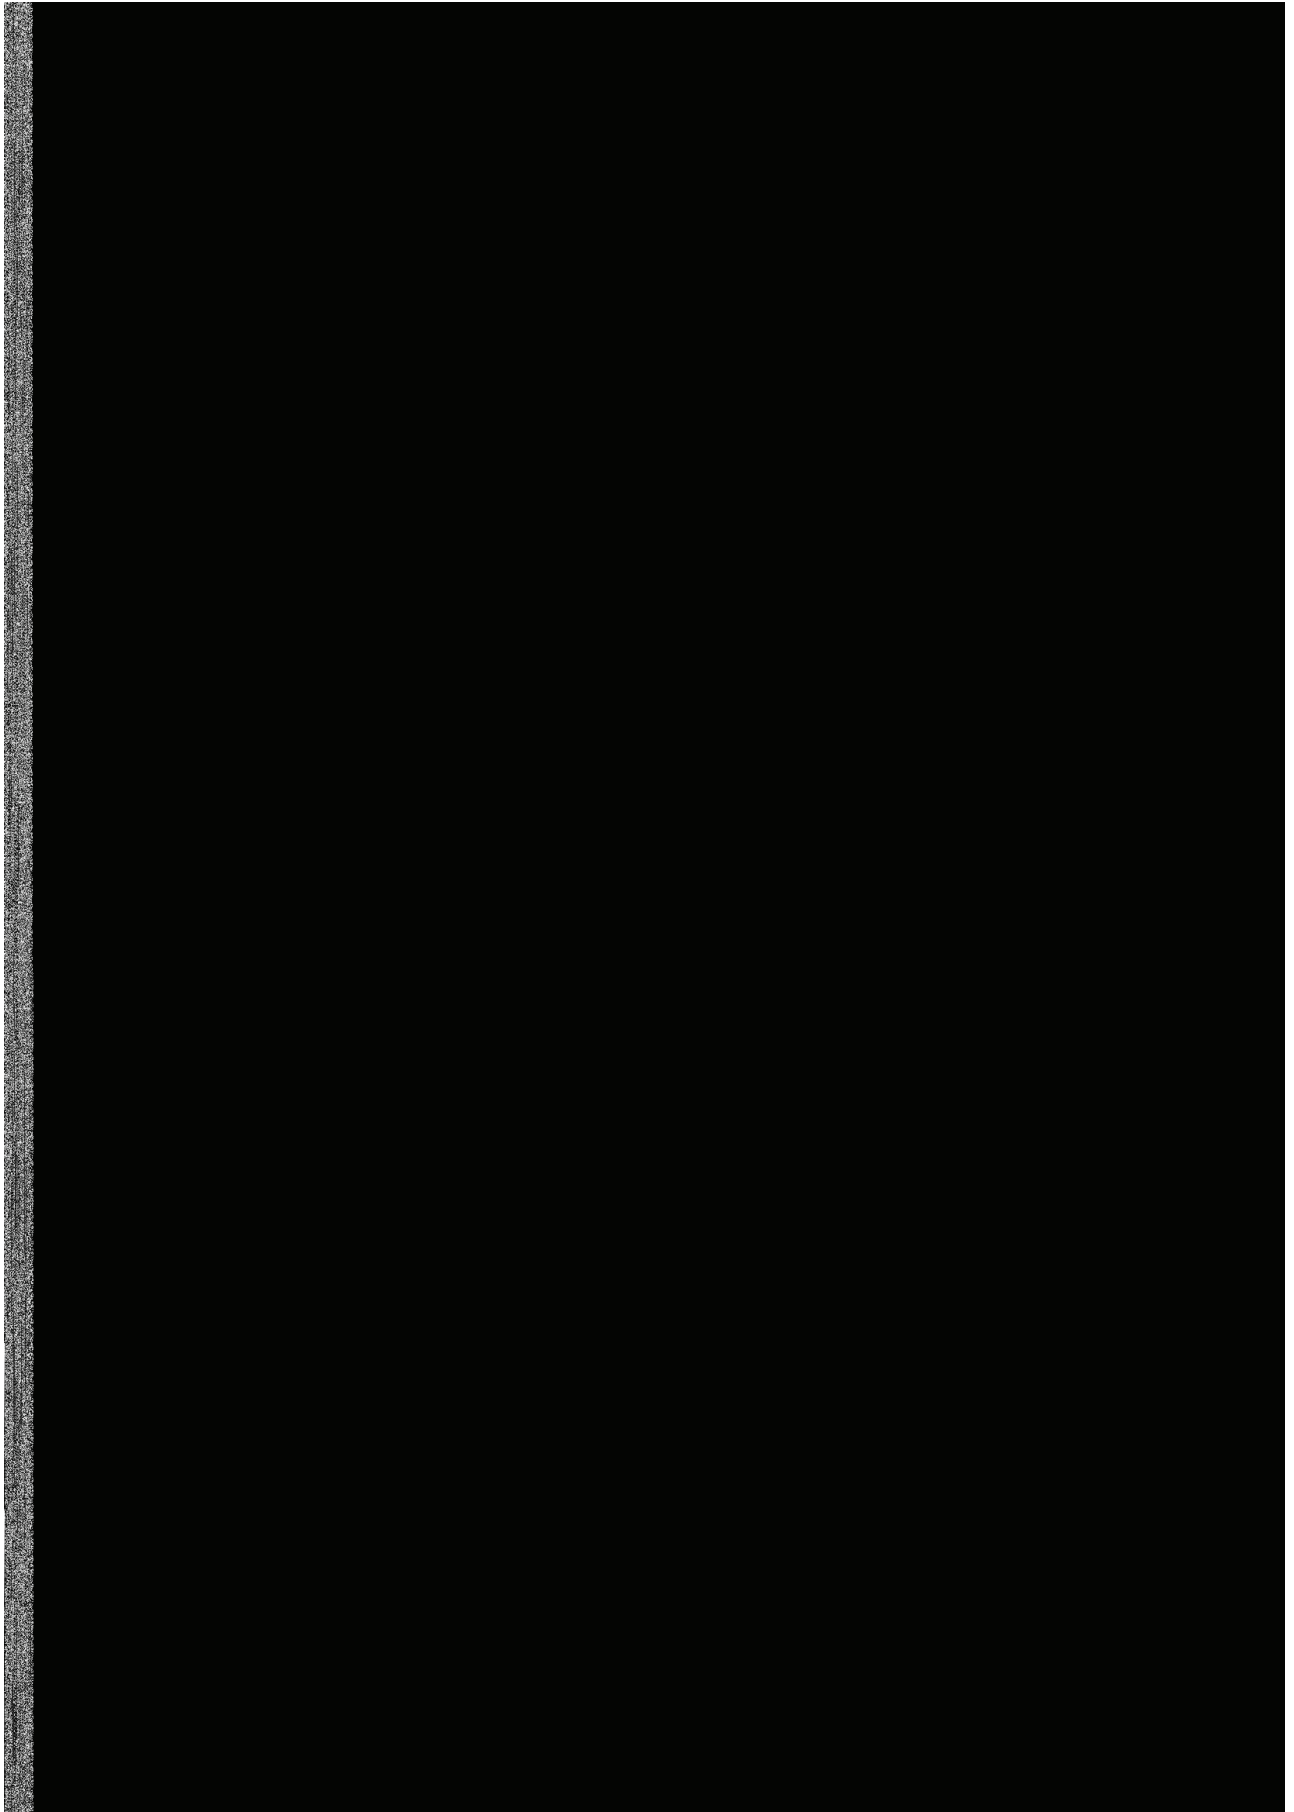


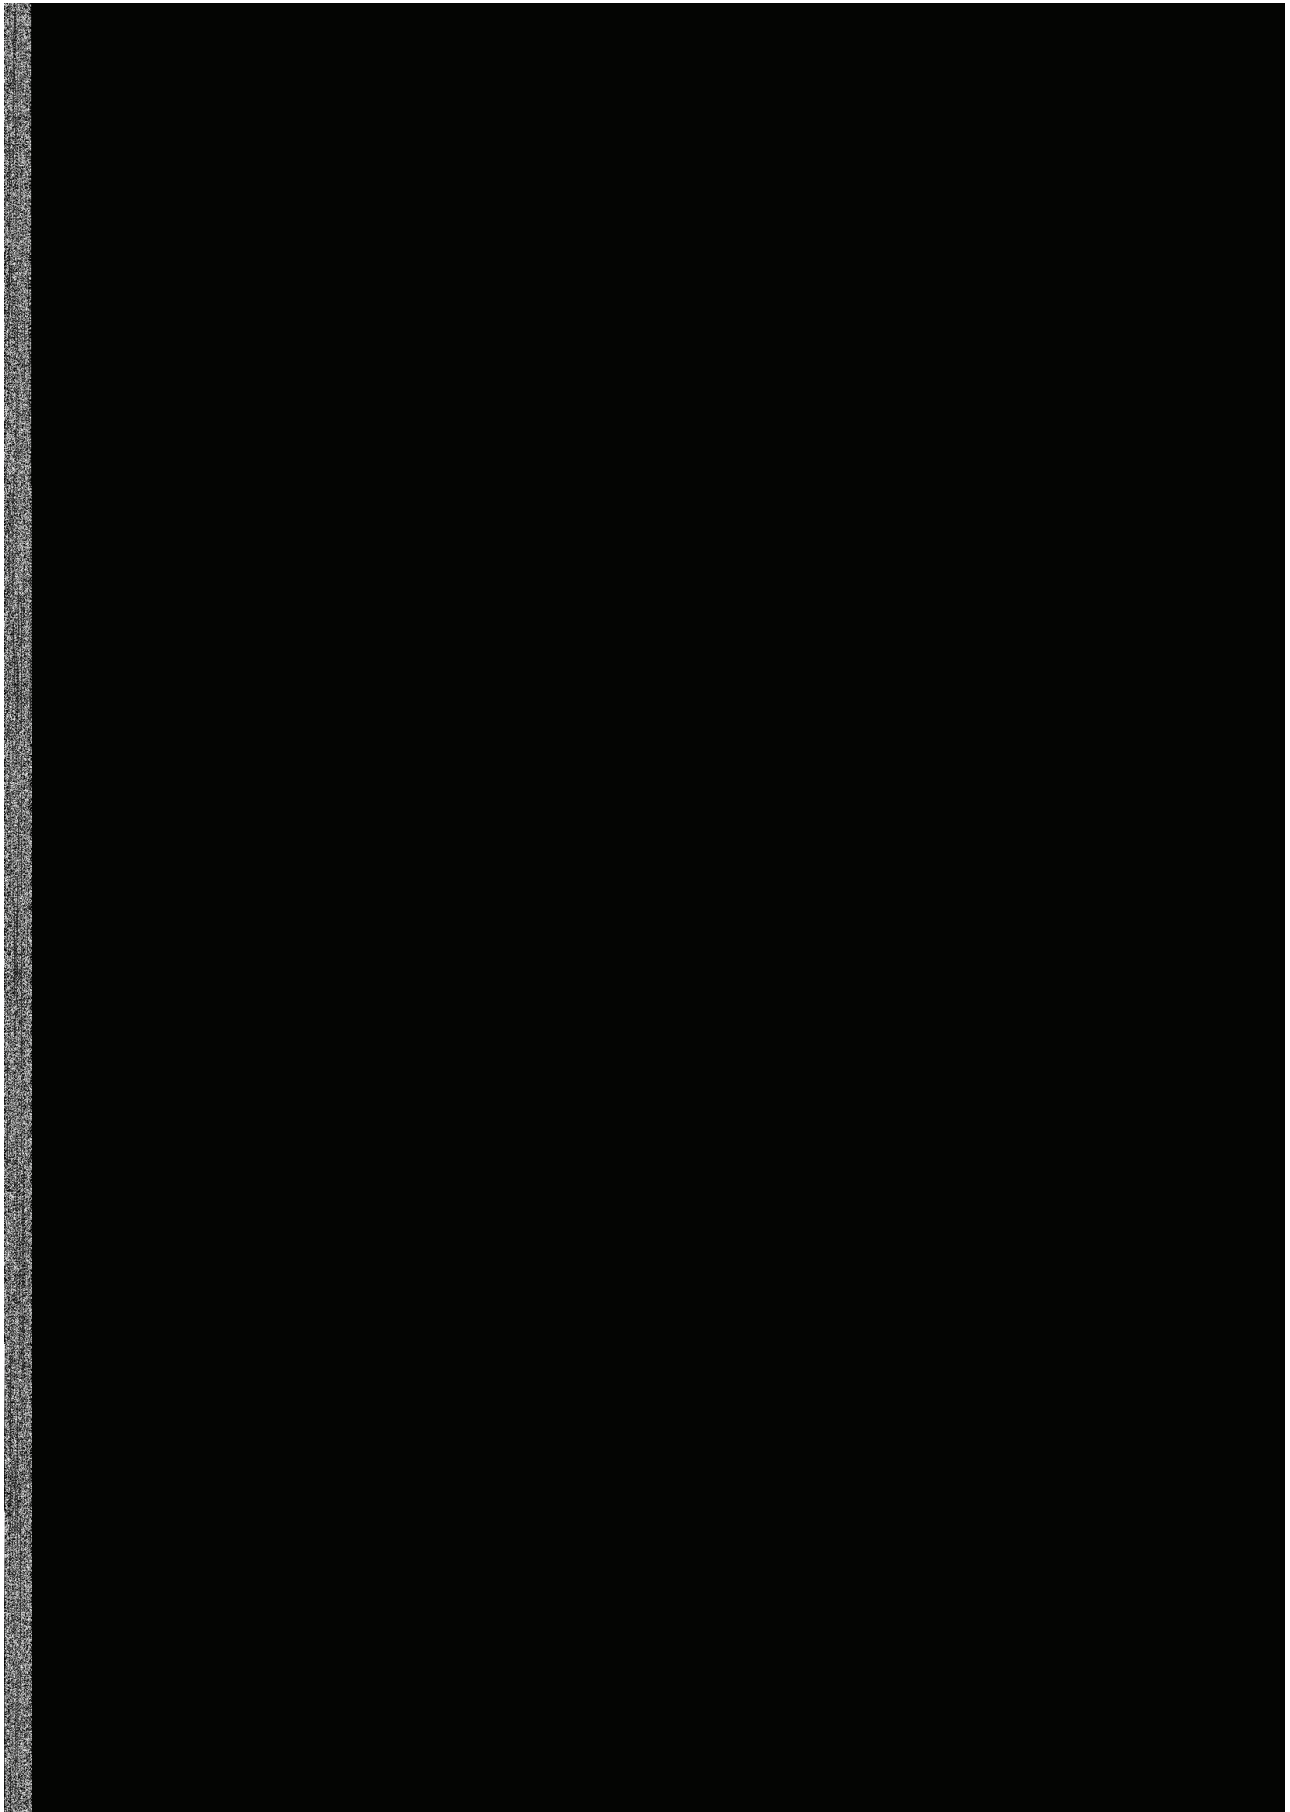





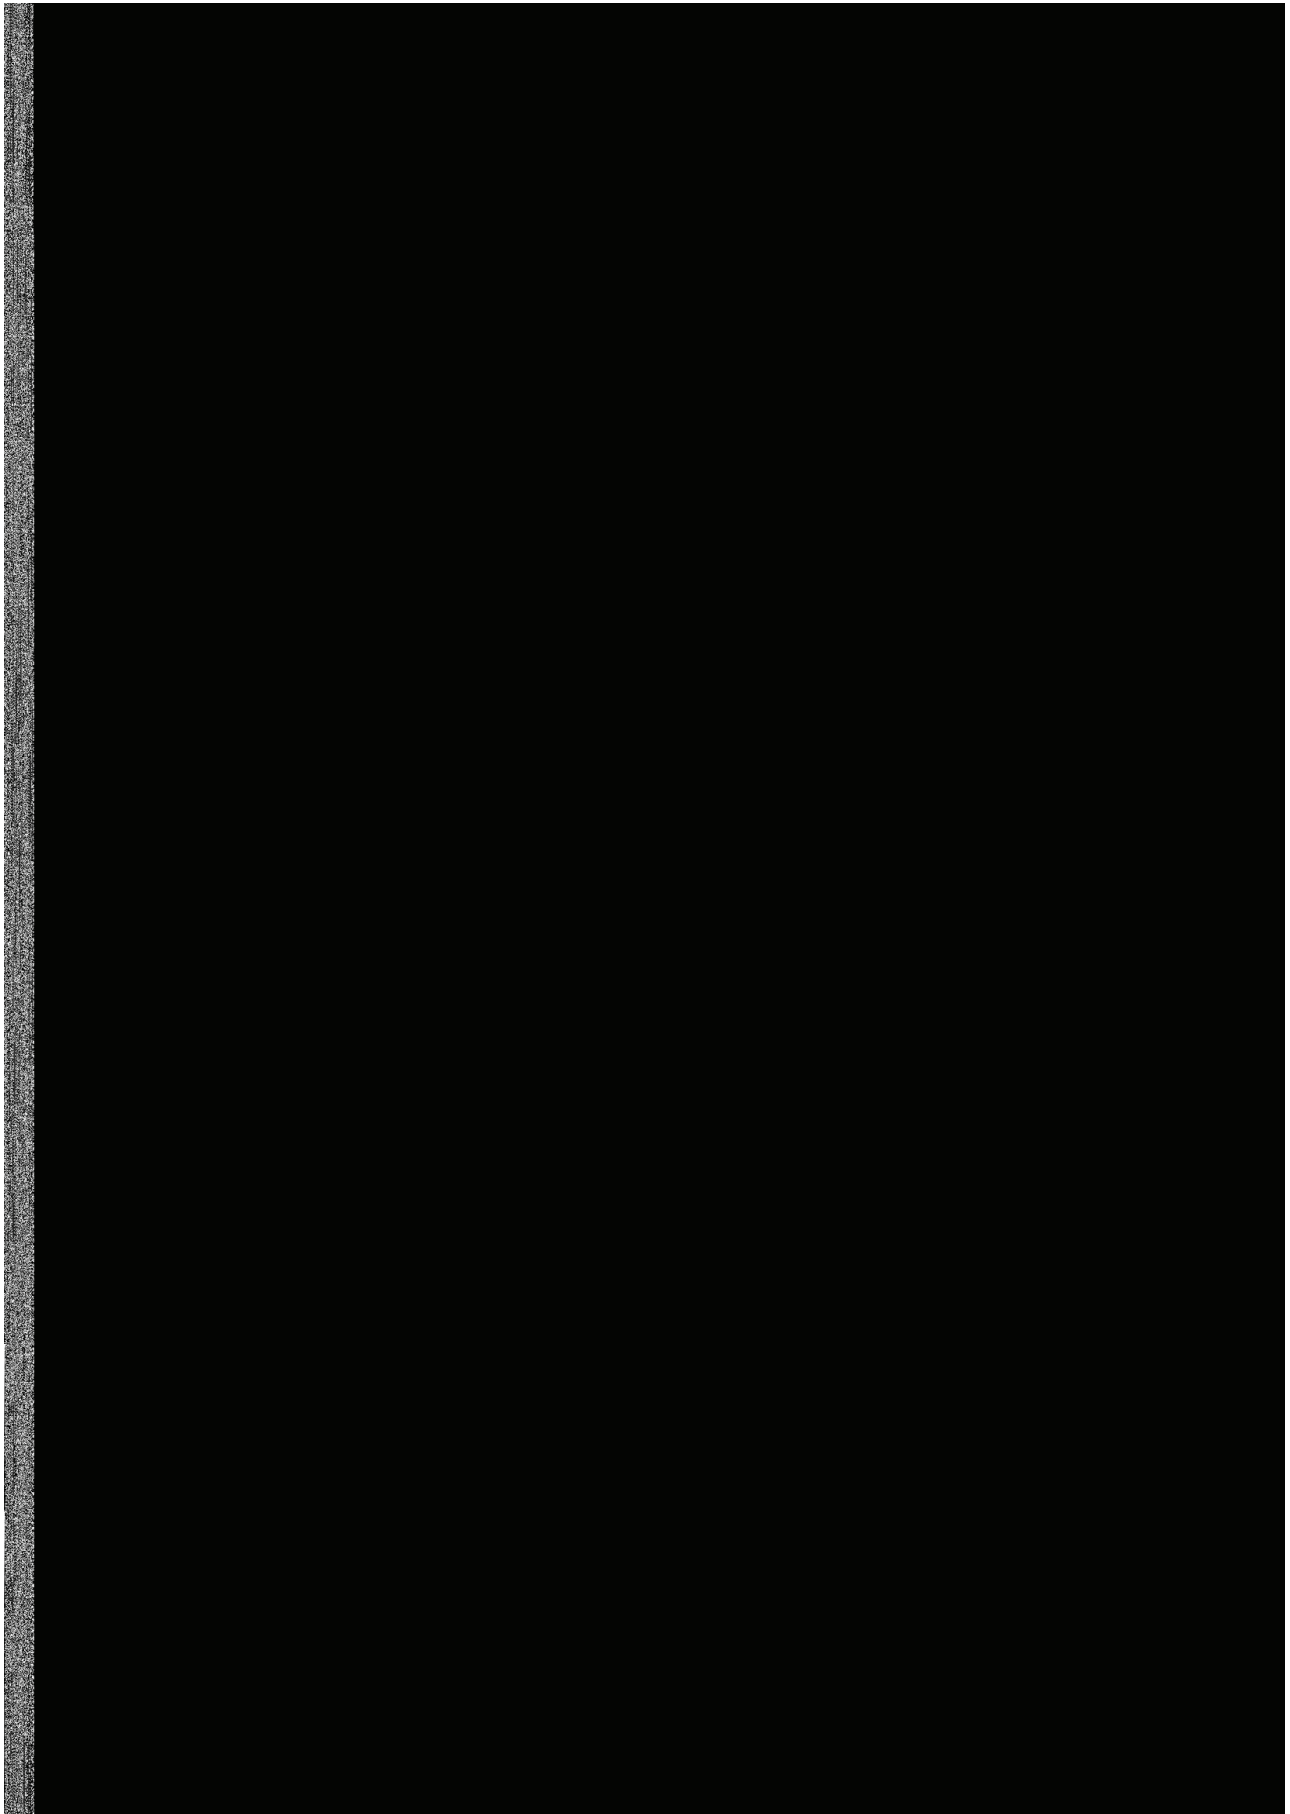


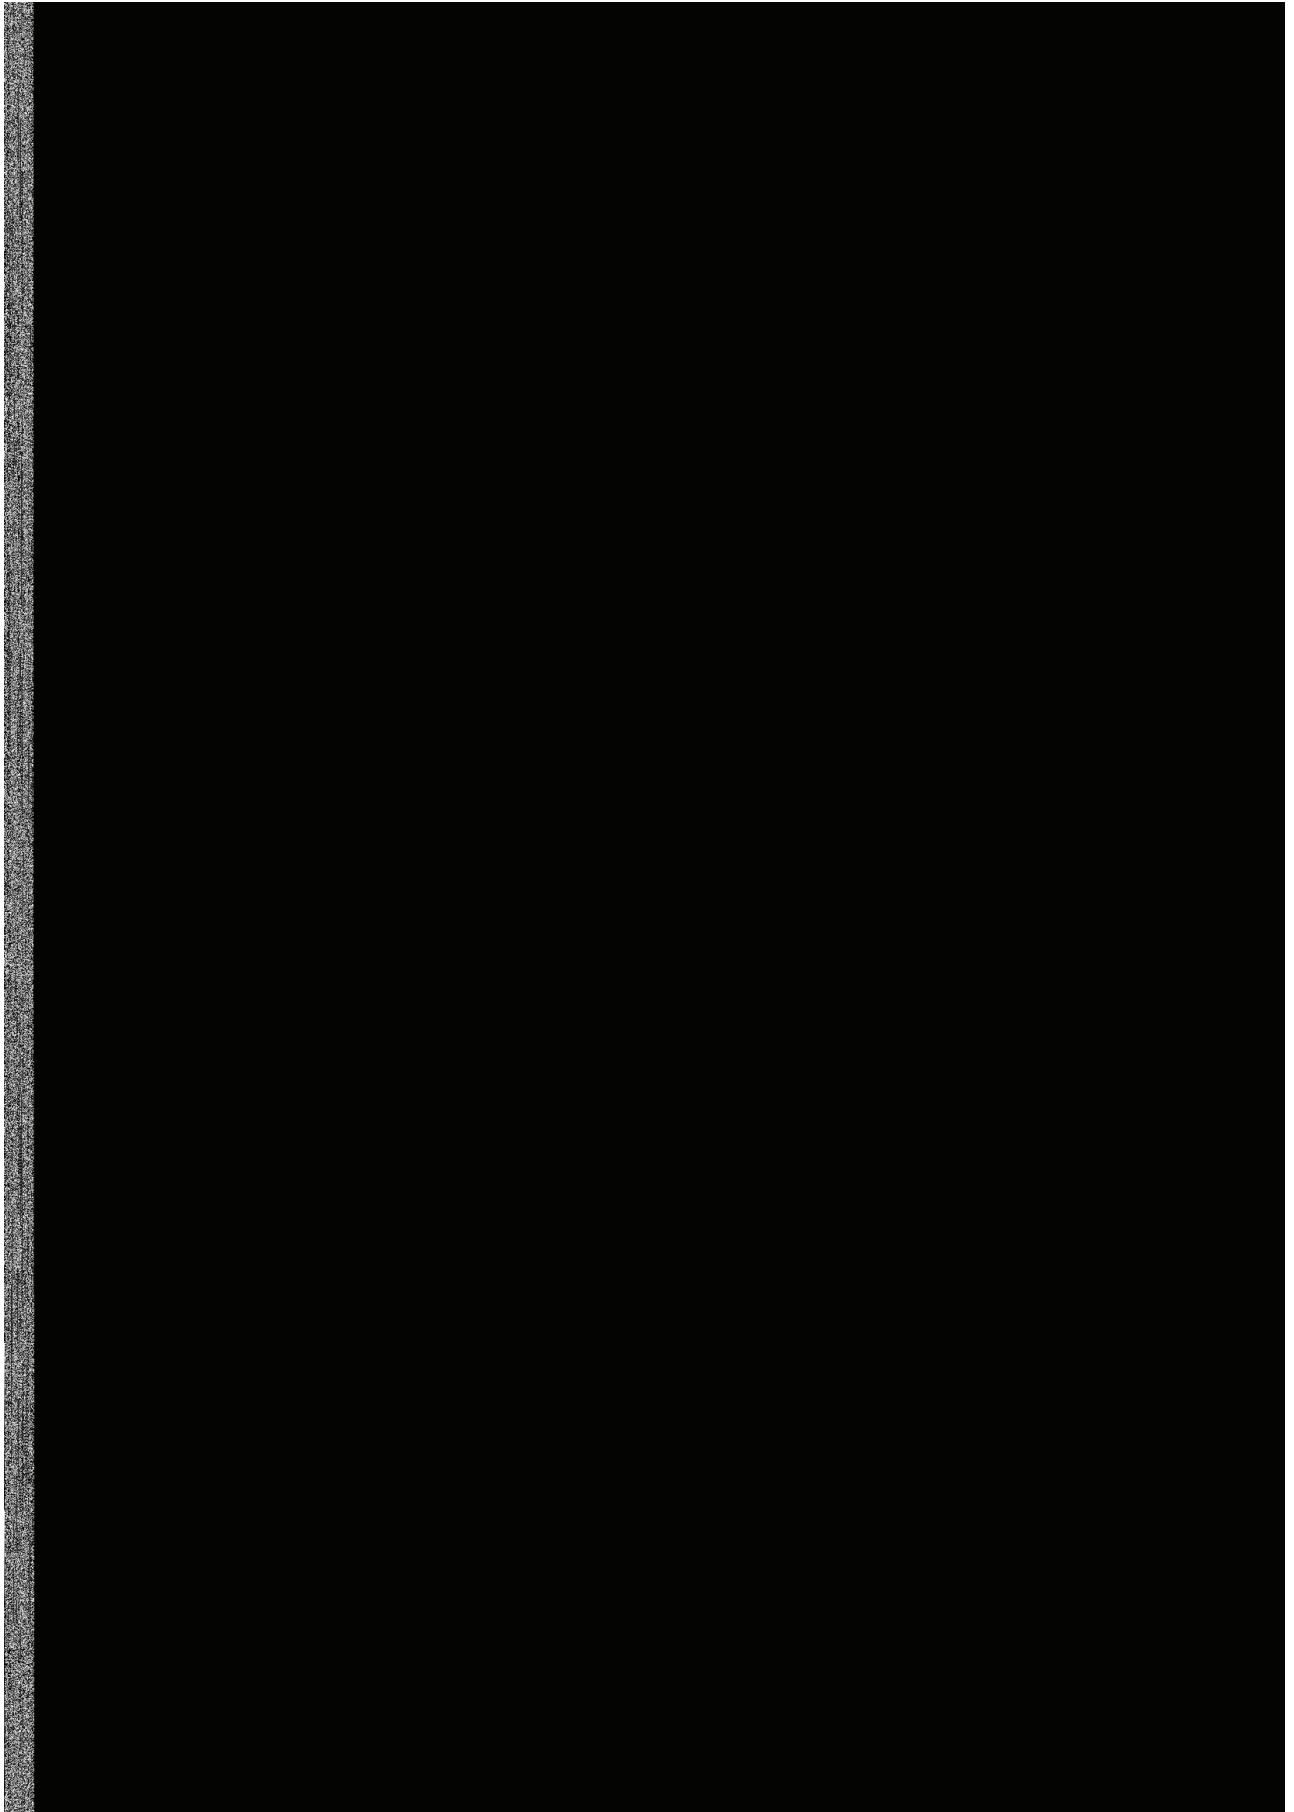


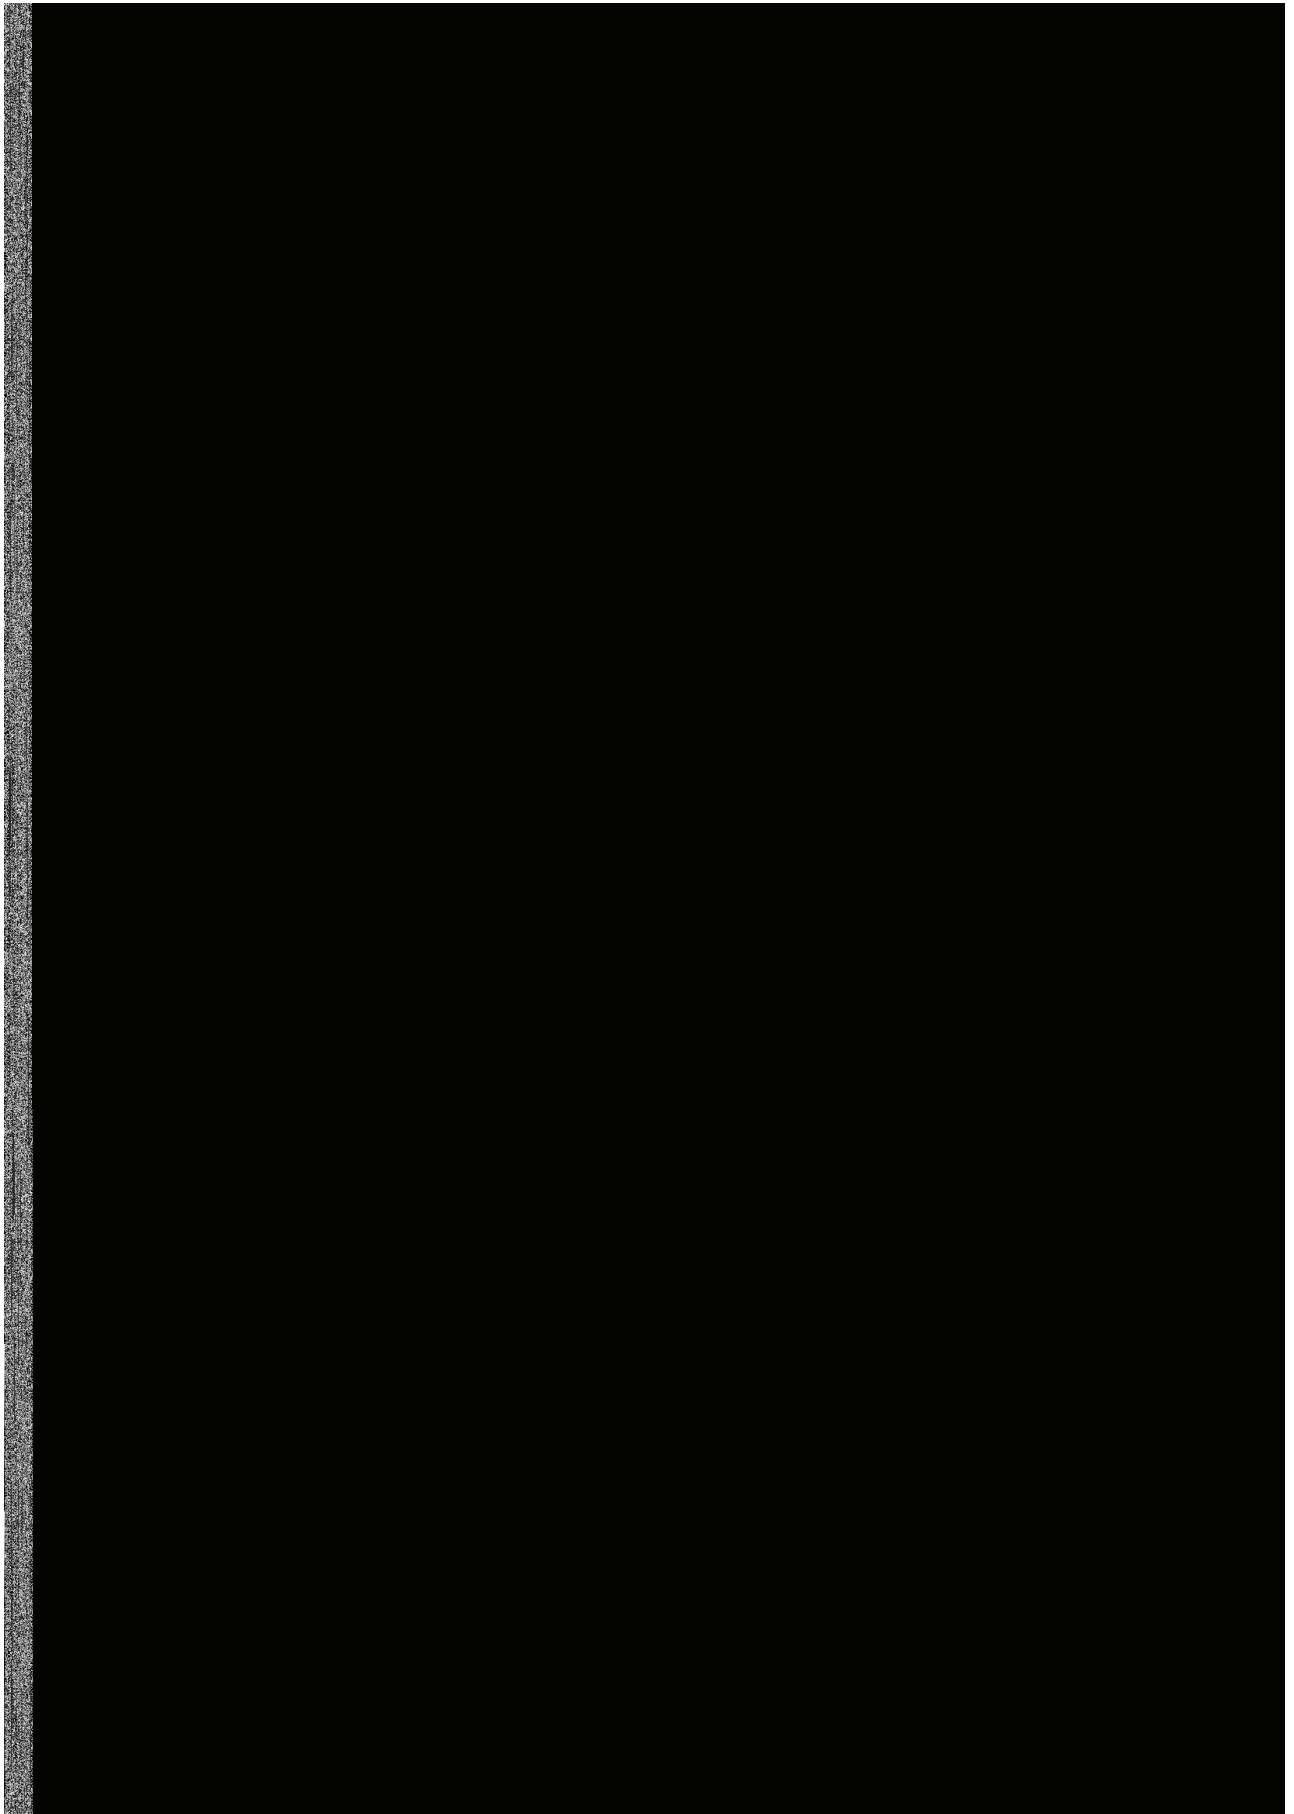


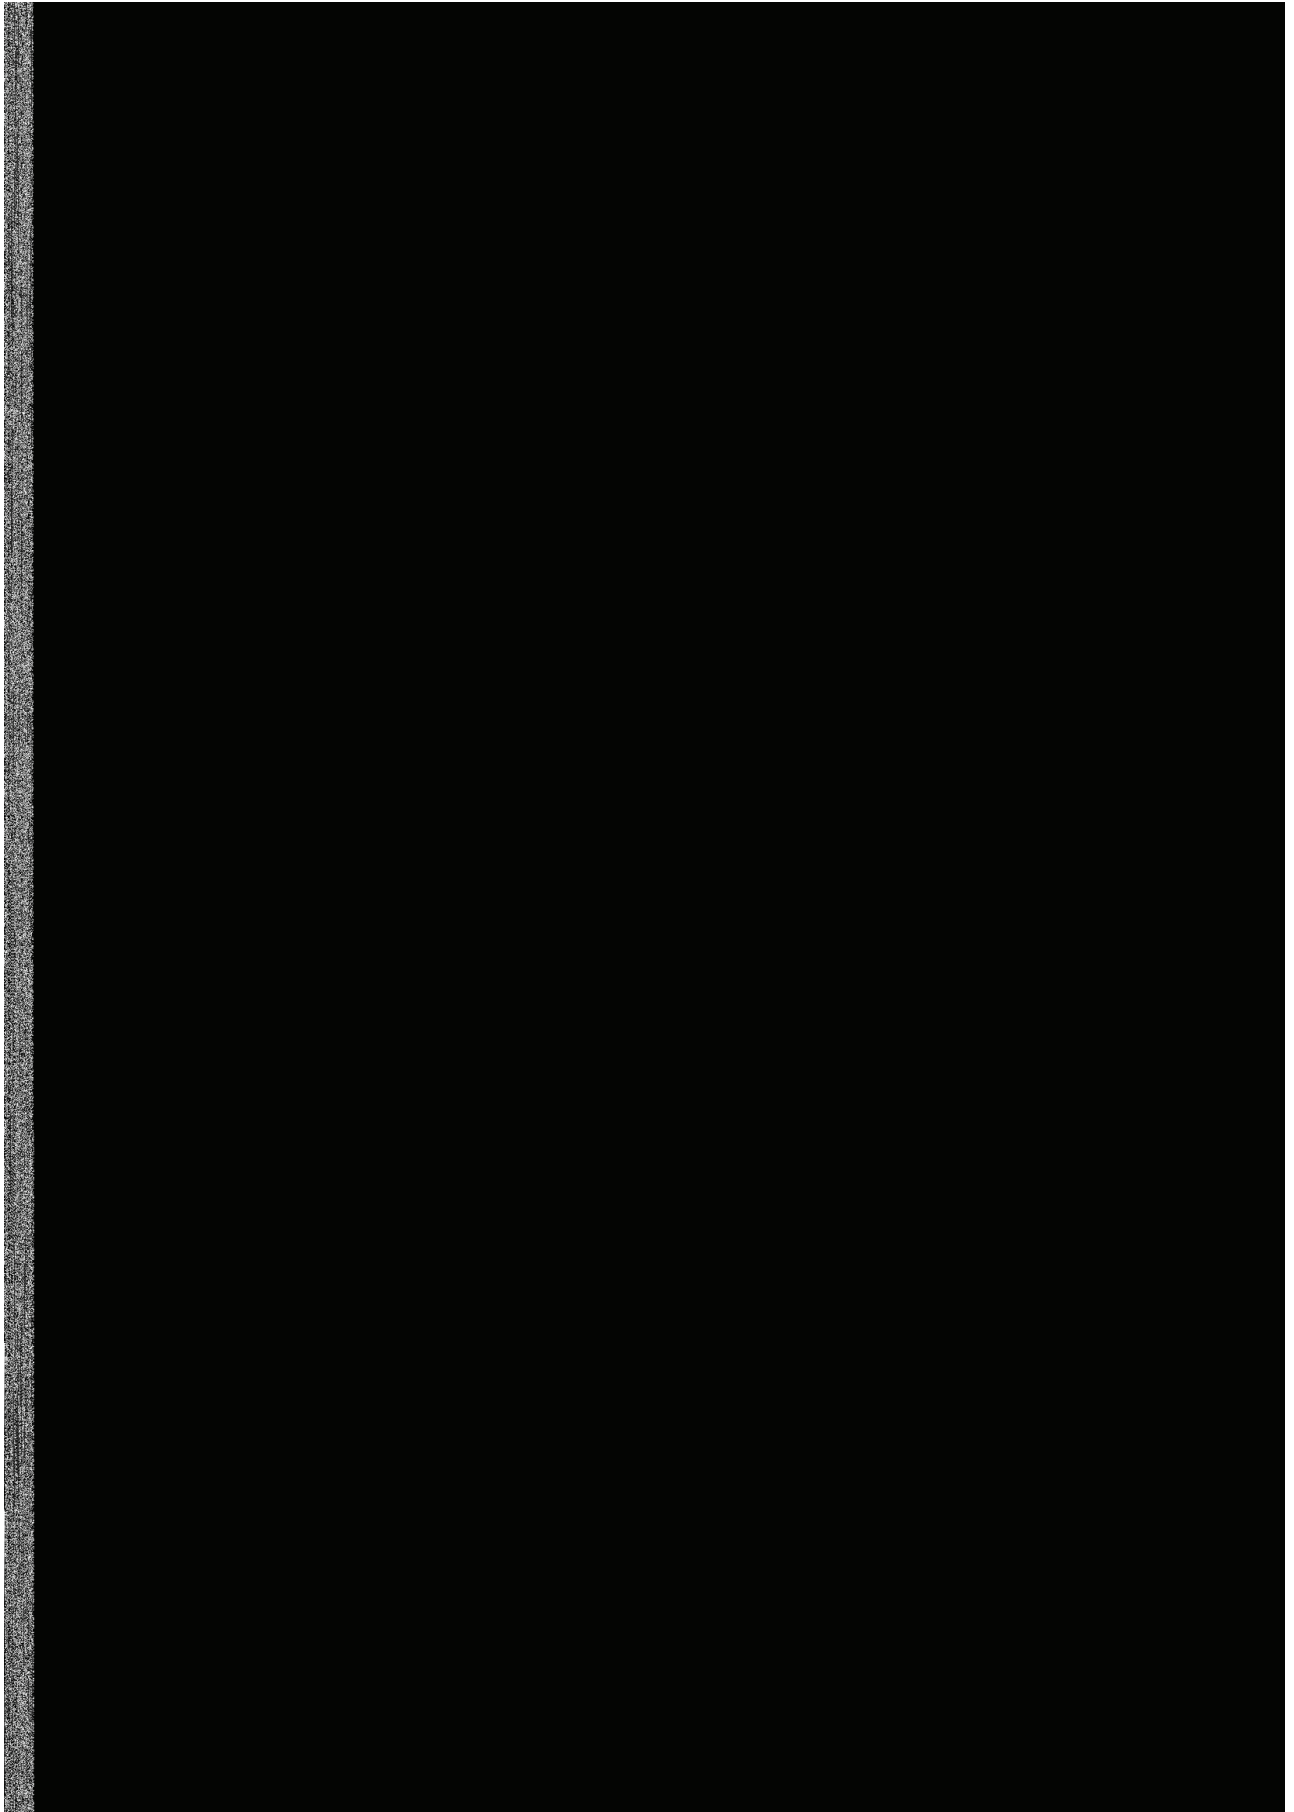


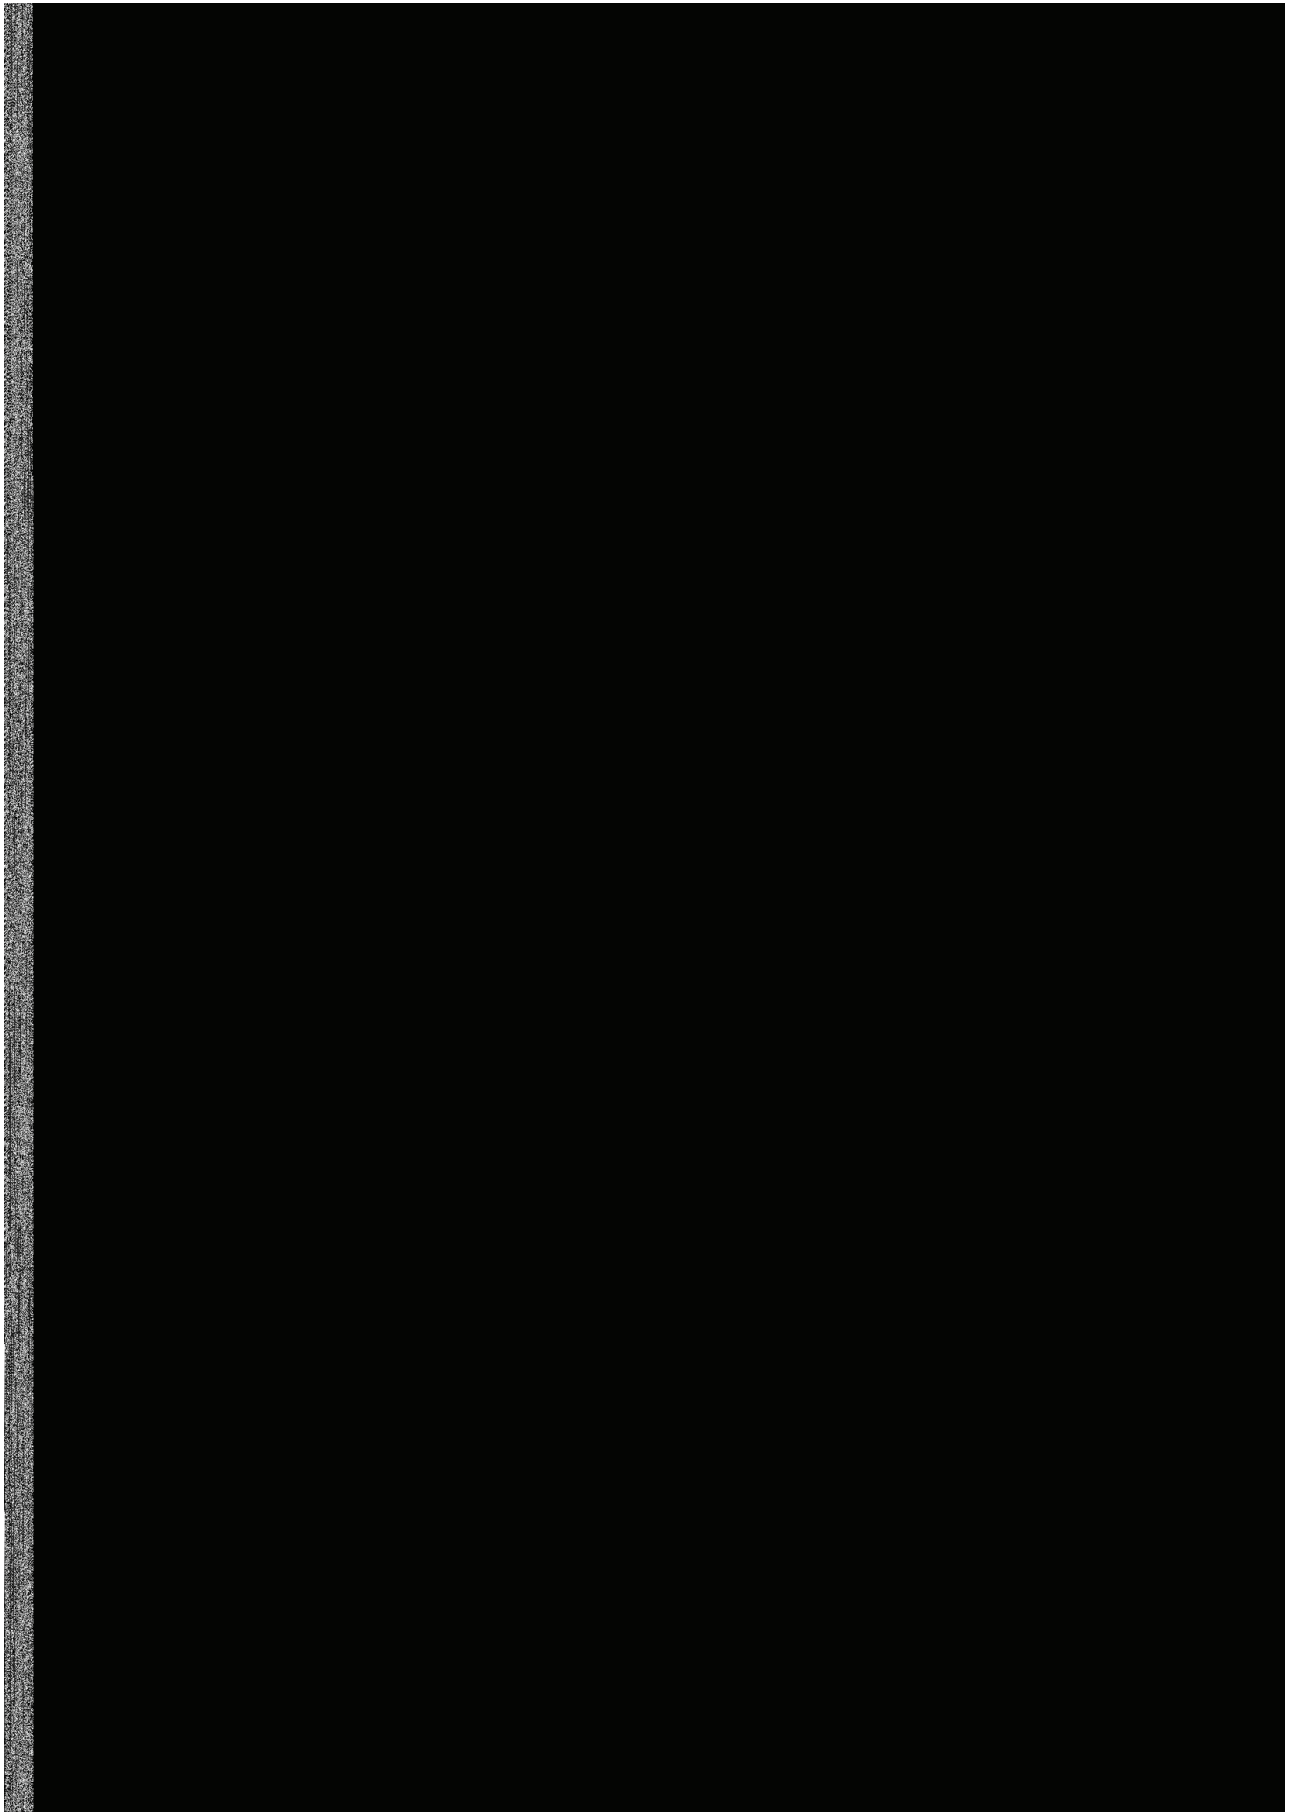


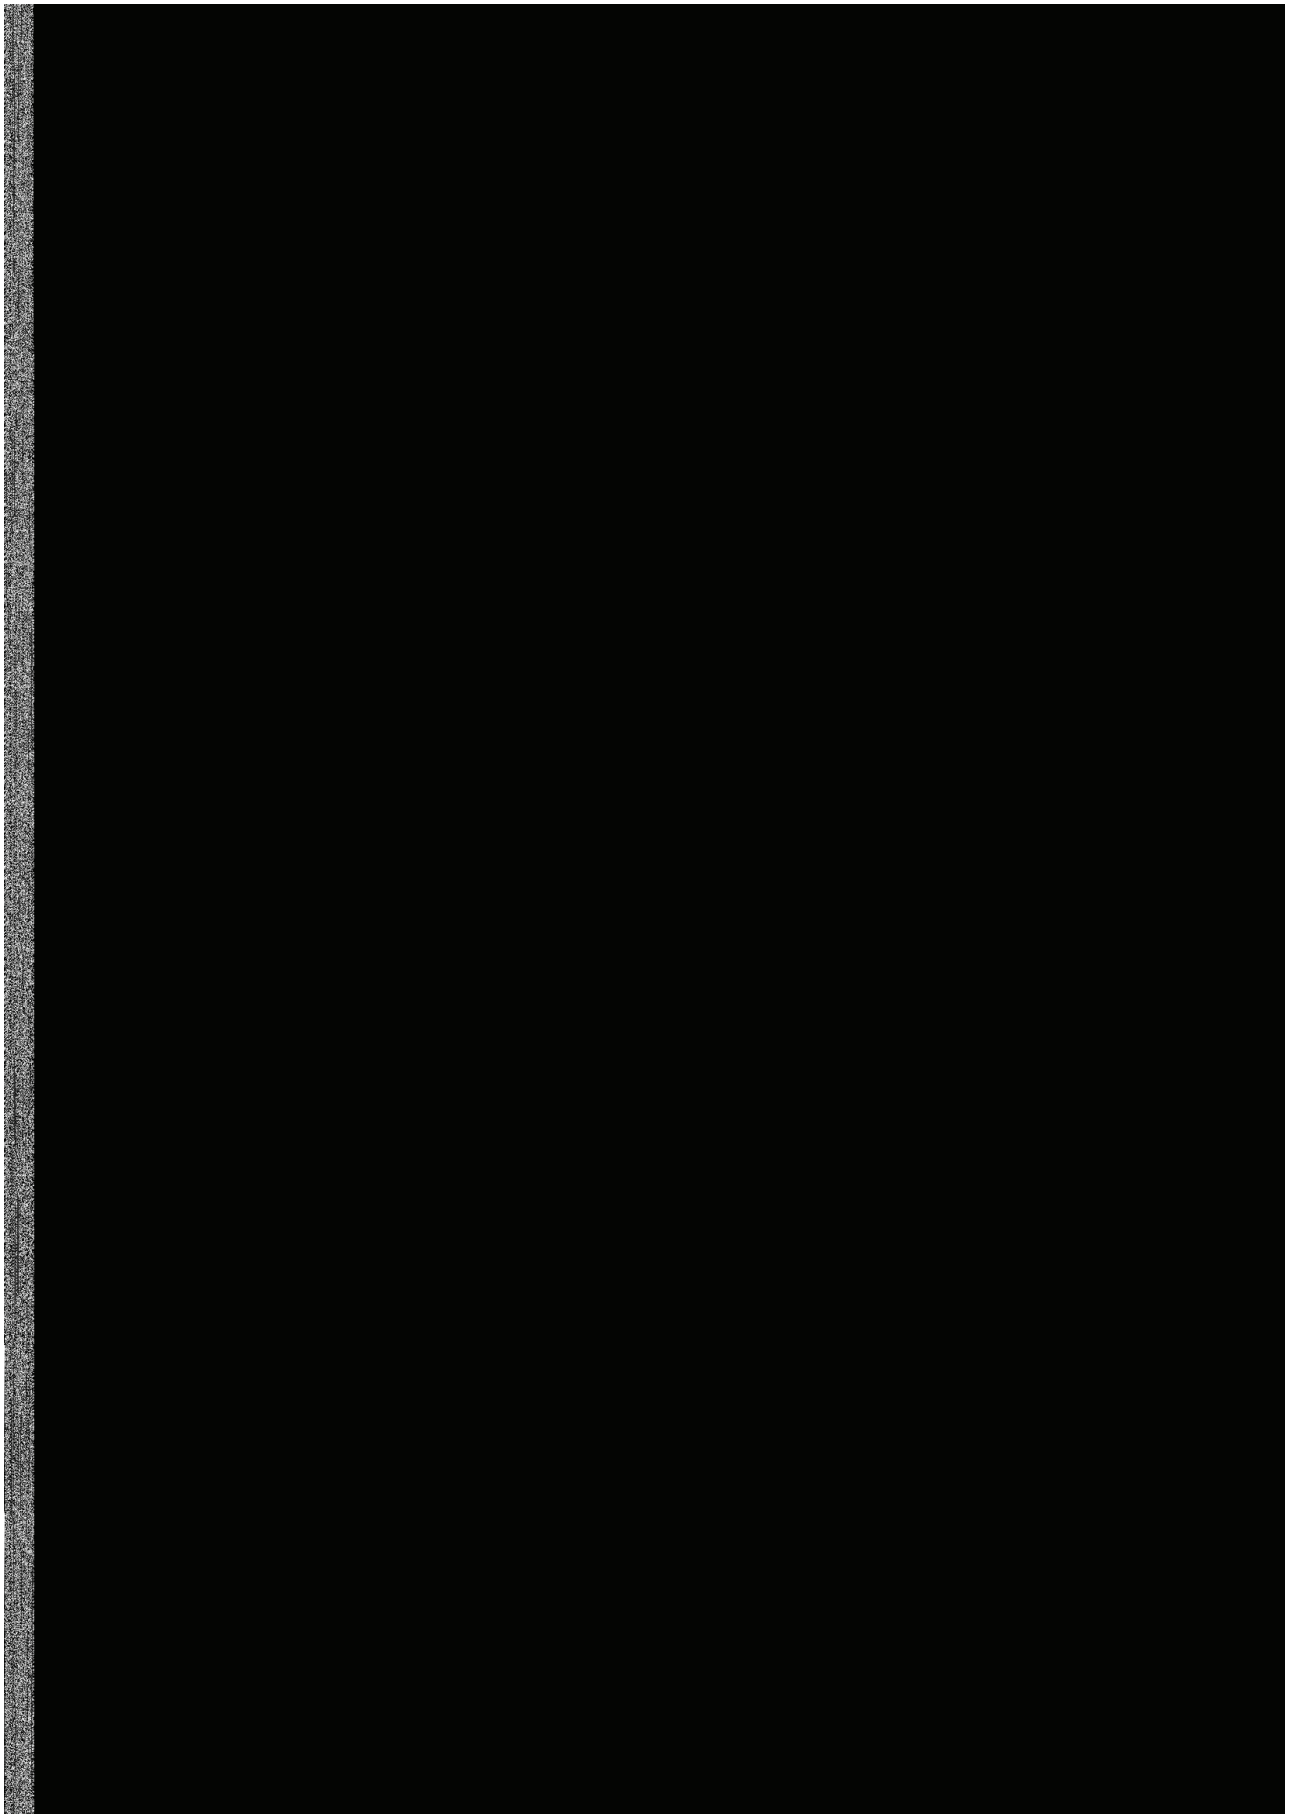

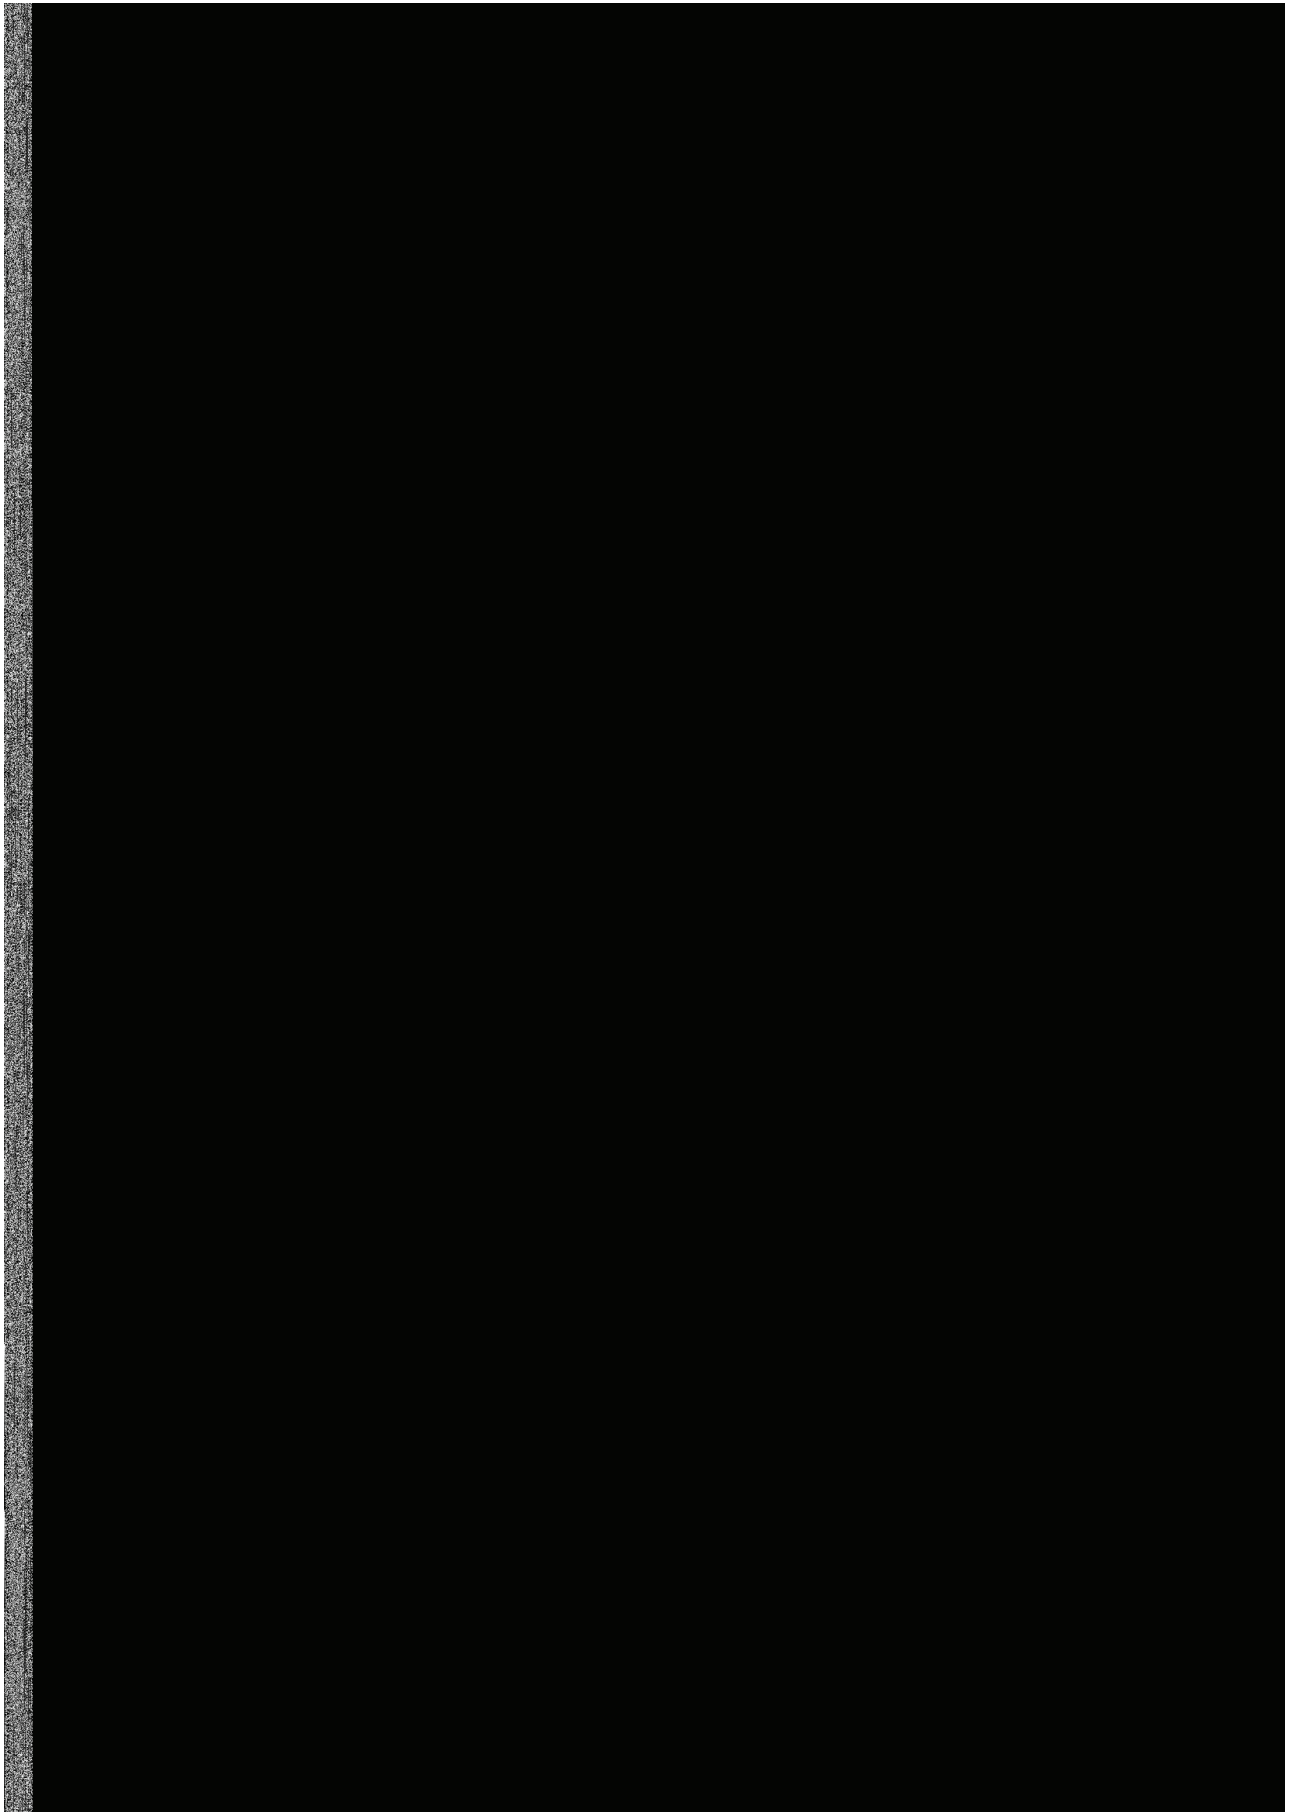


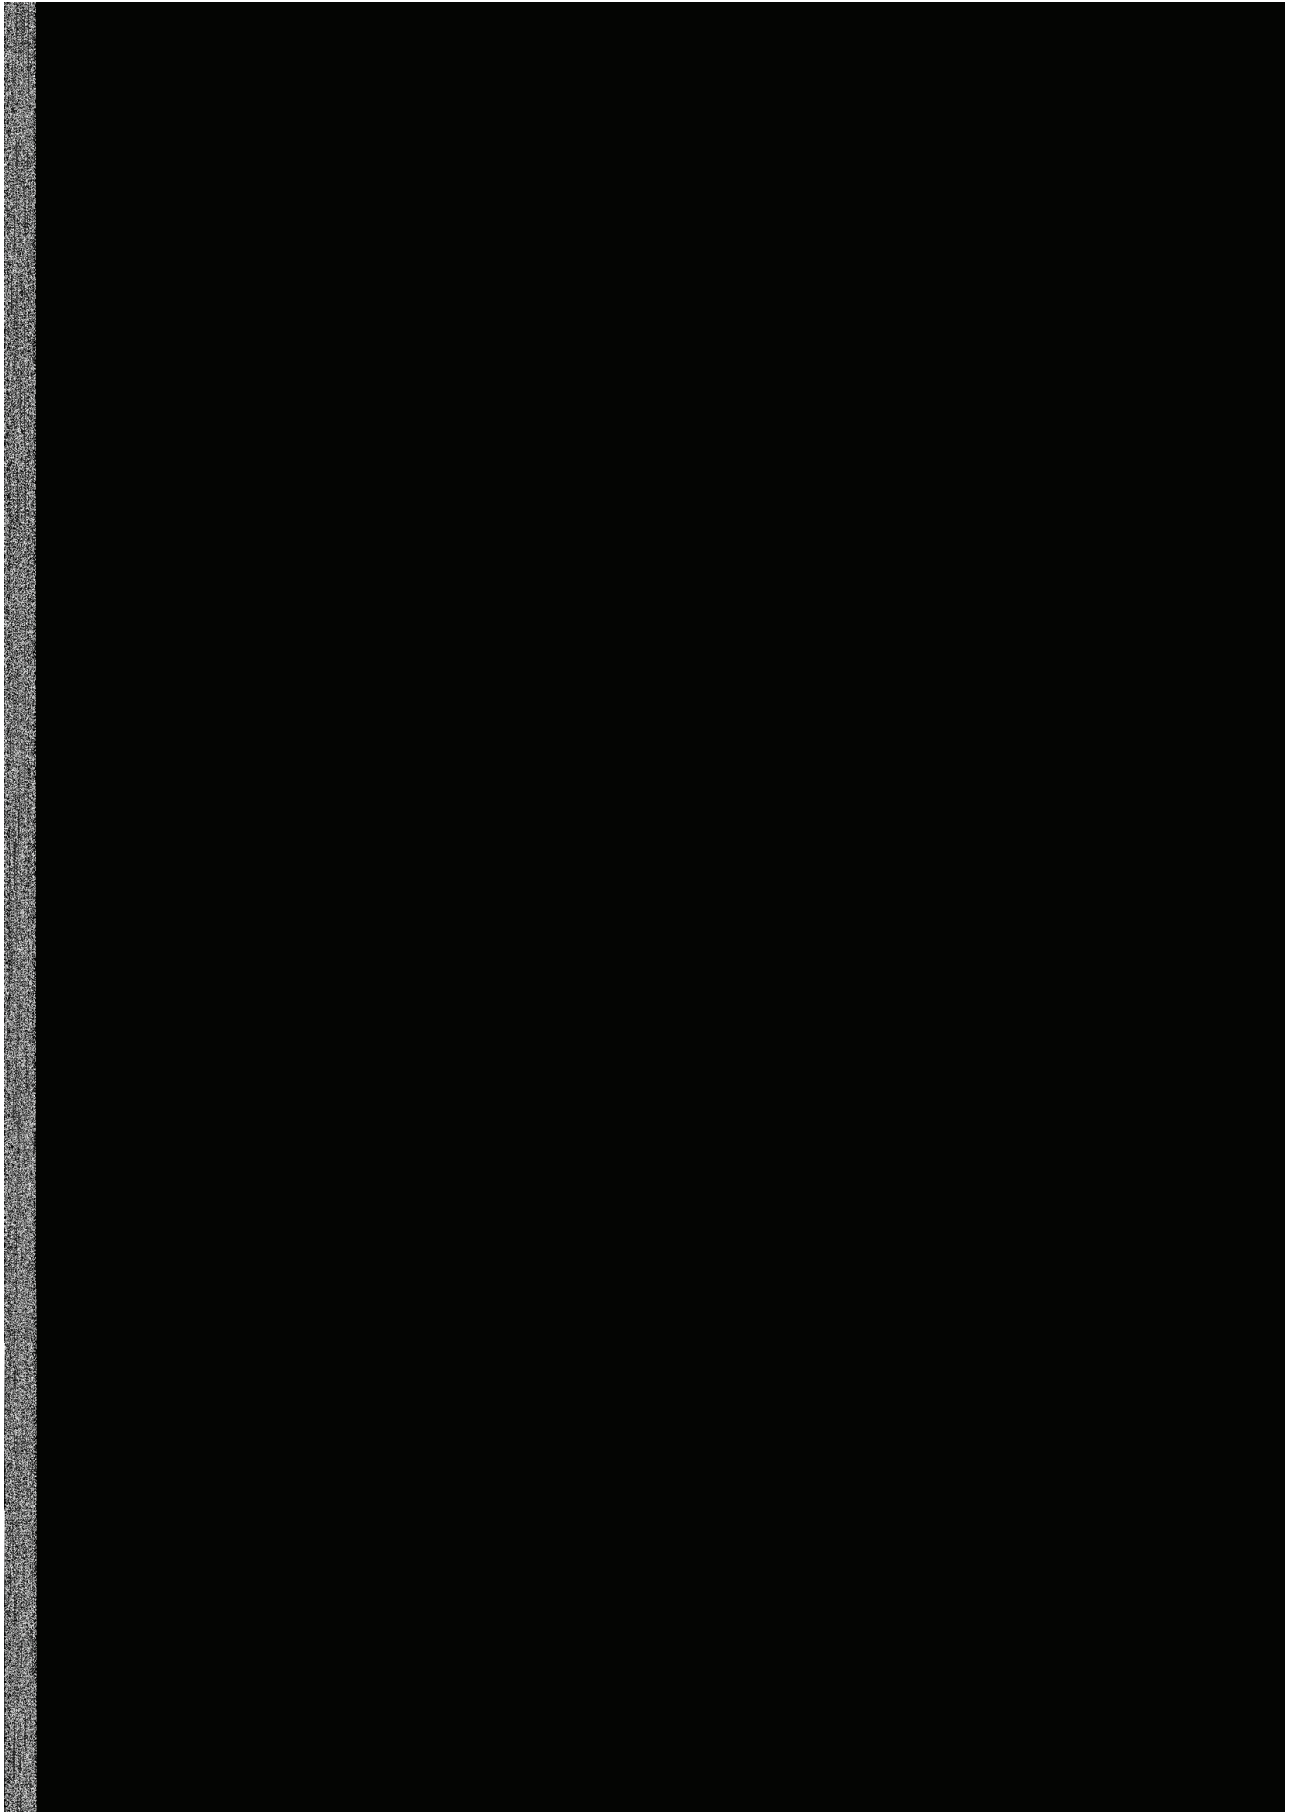


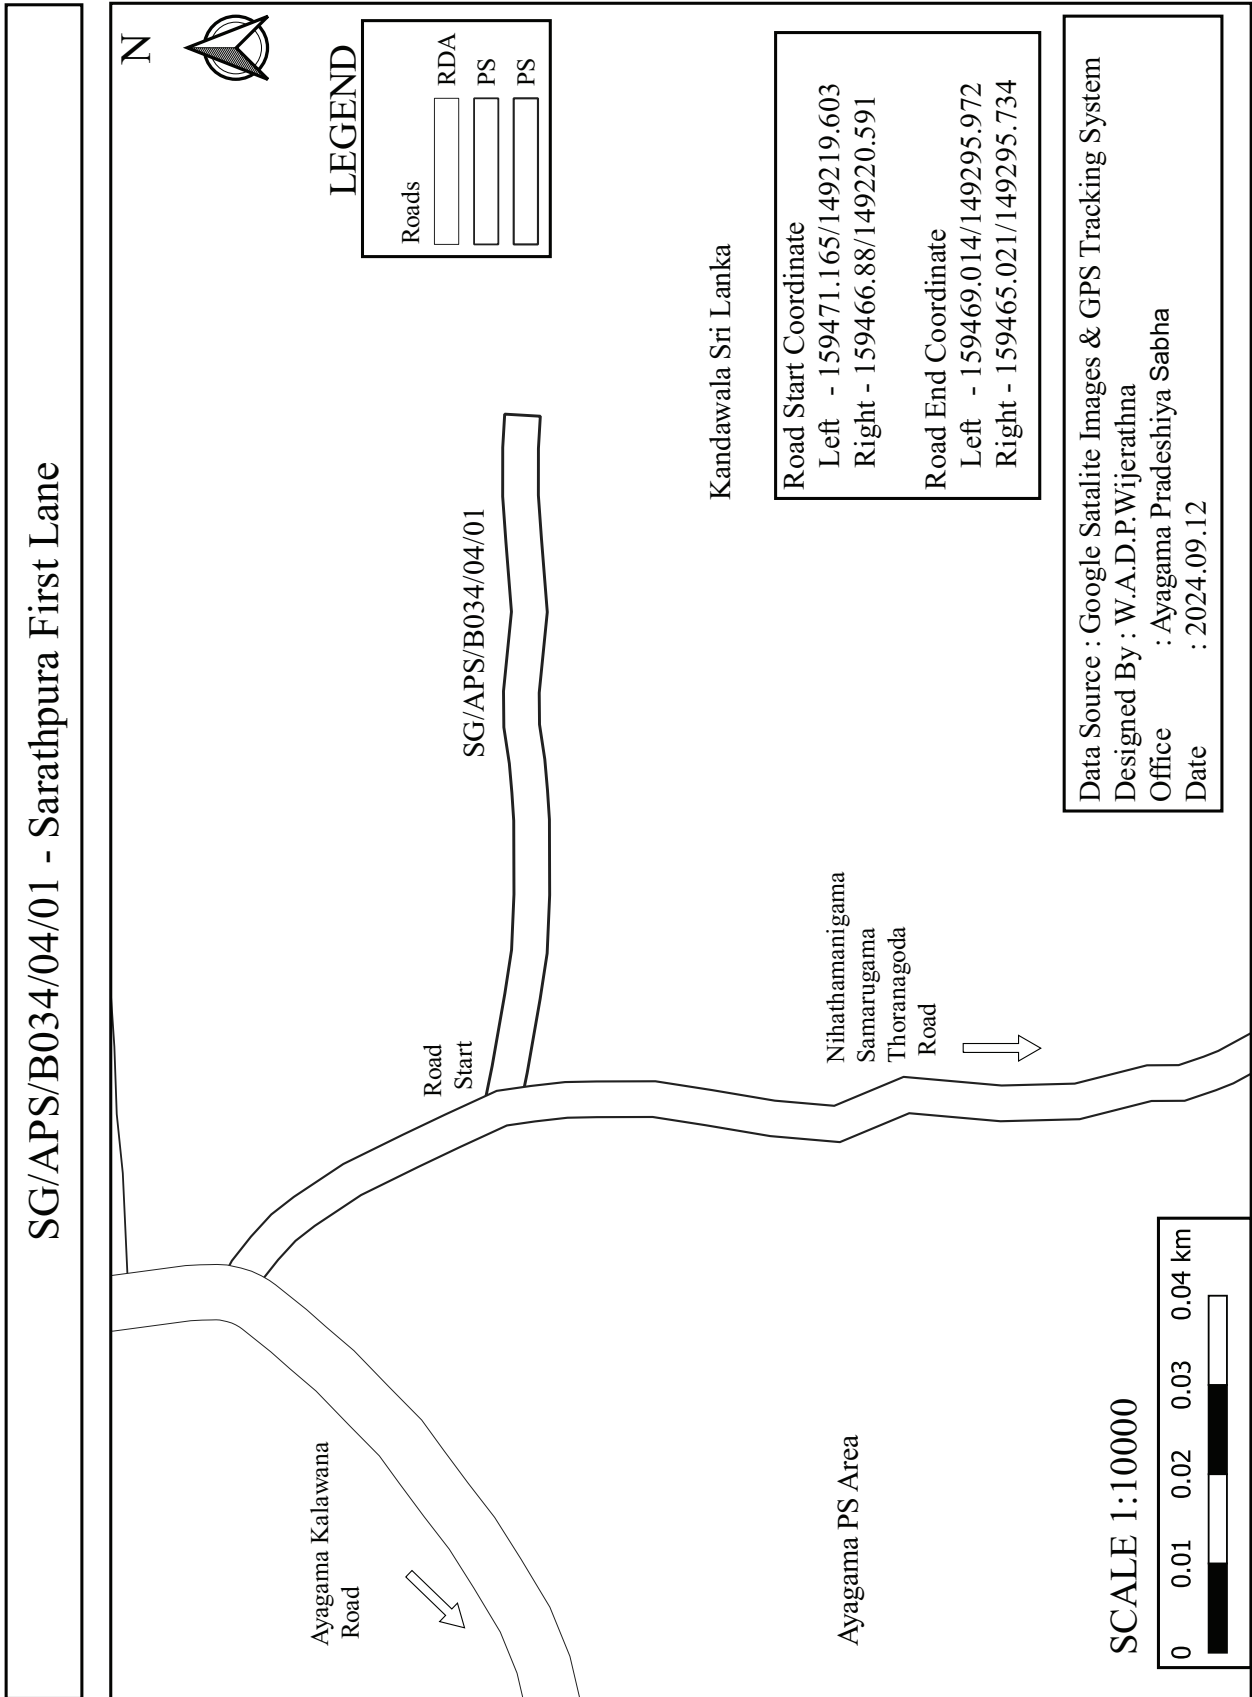


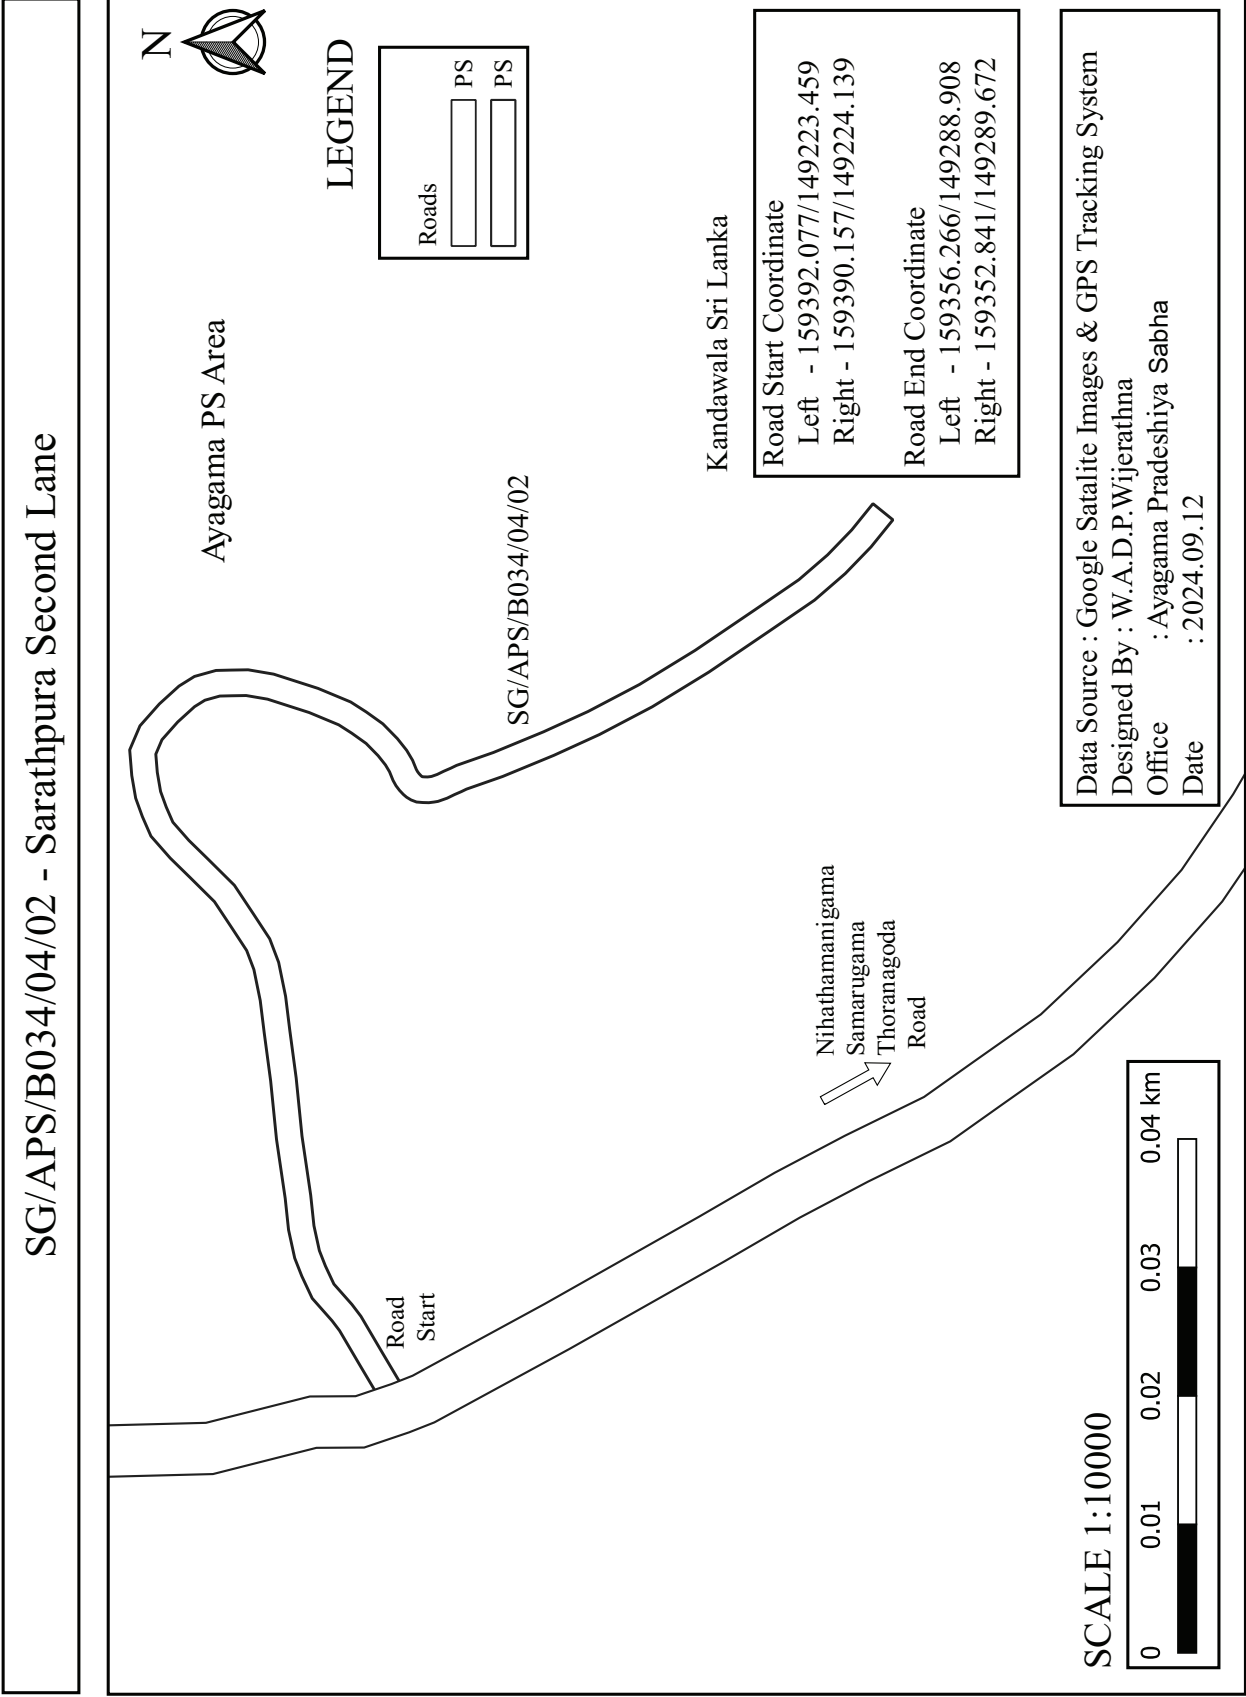



SG/APS/B034/04/03 - Koratuwawaththa Road

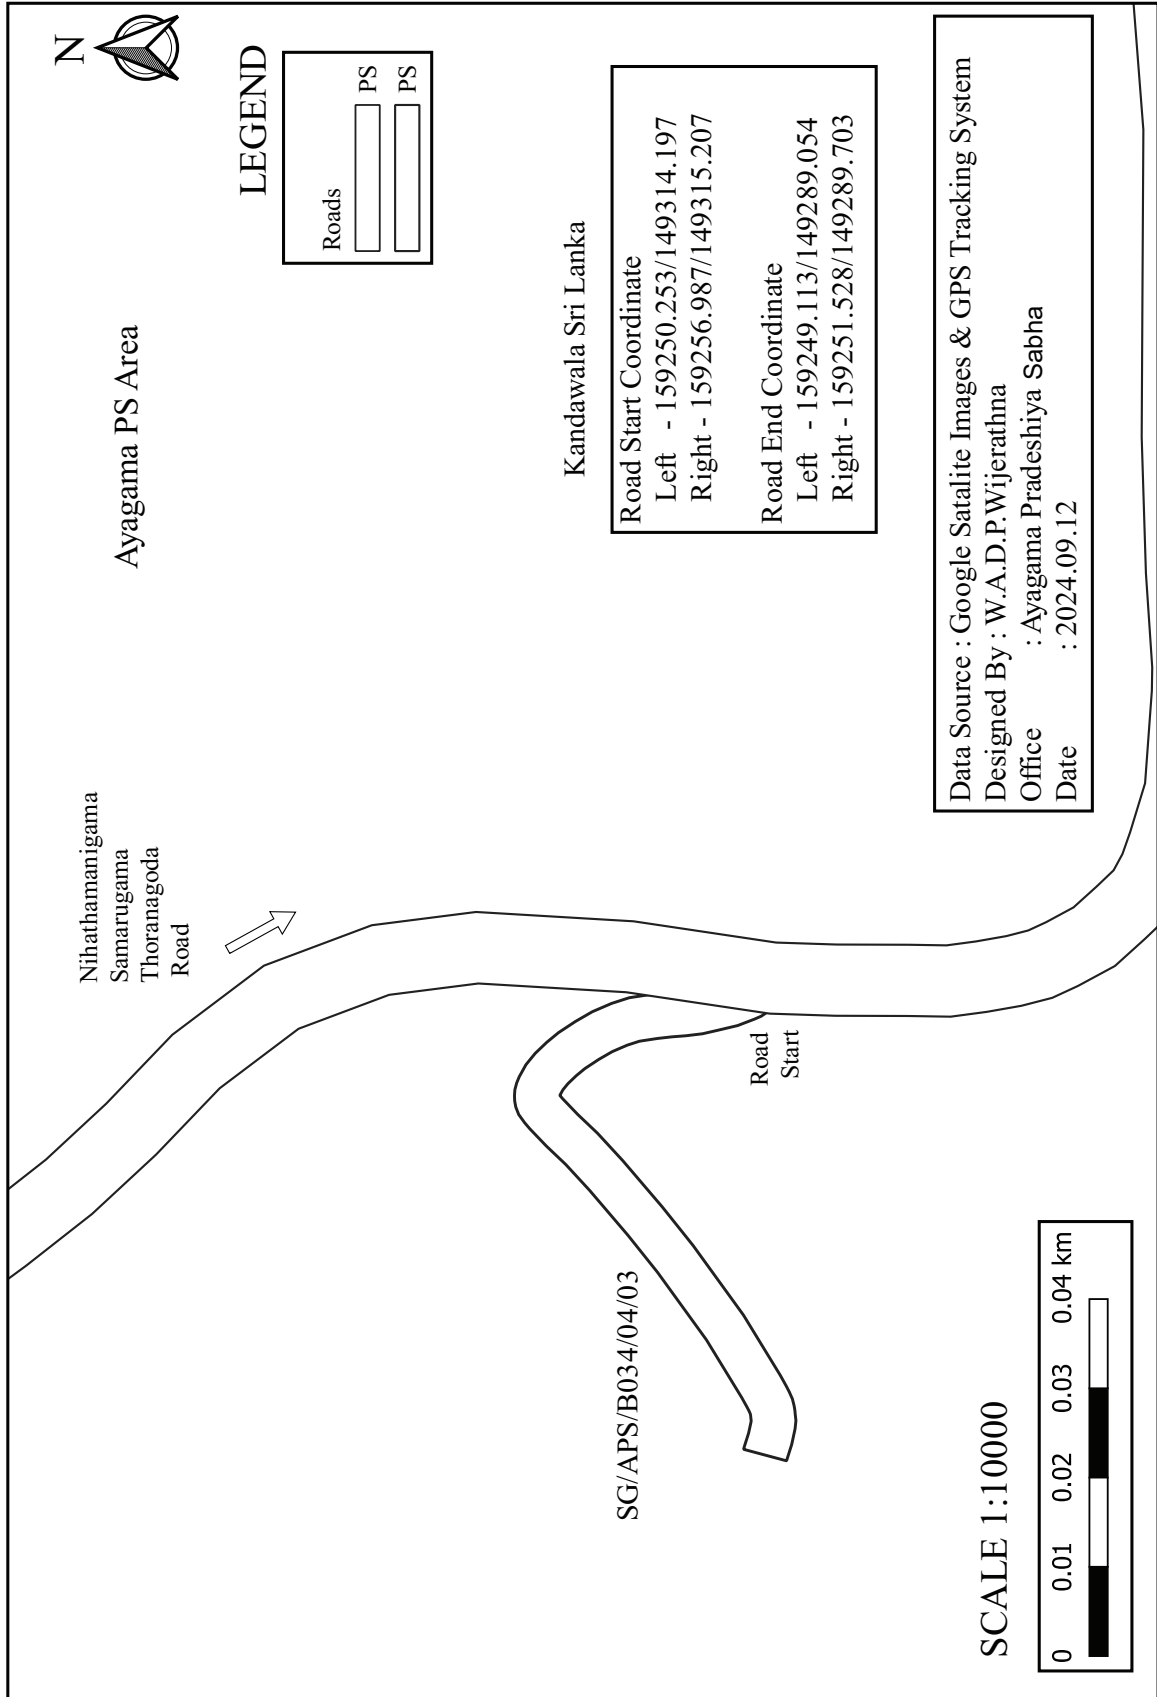


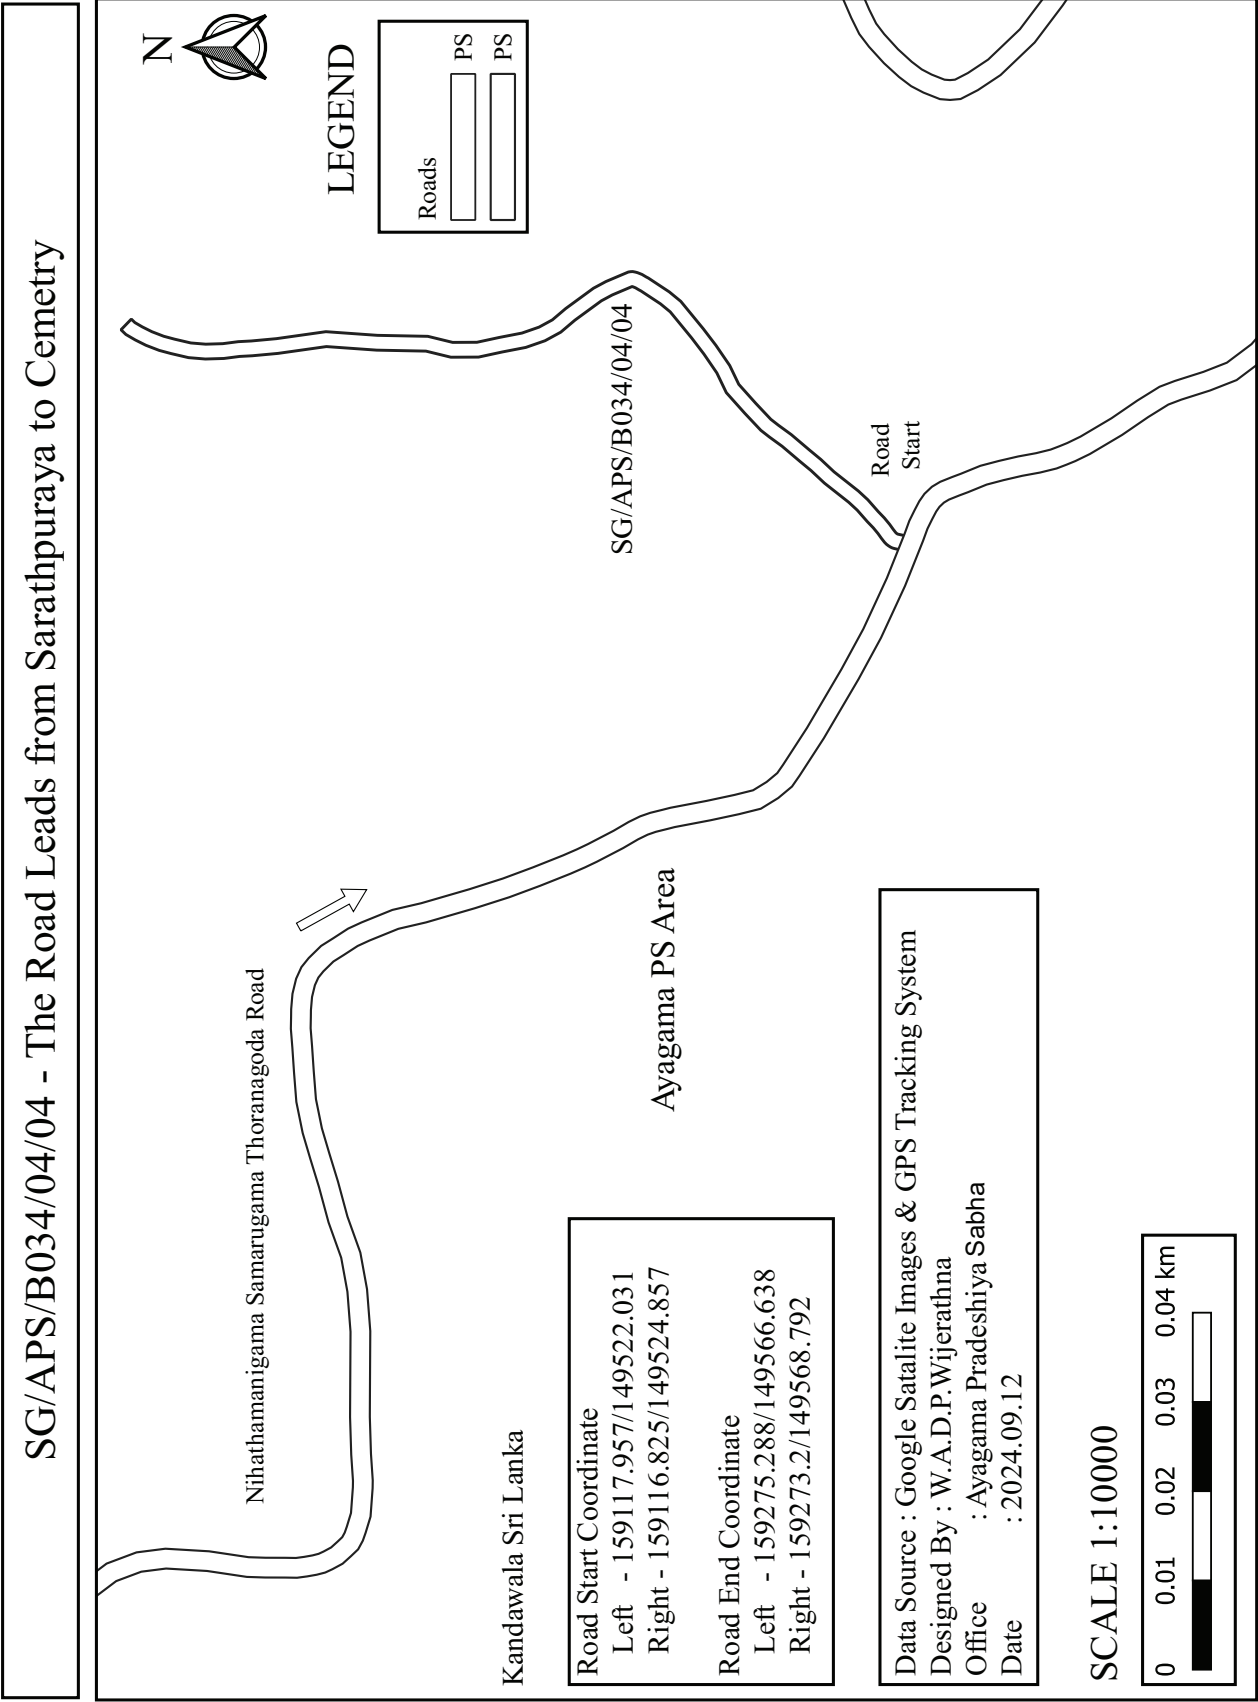


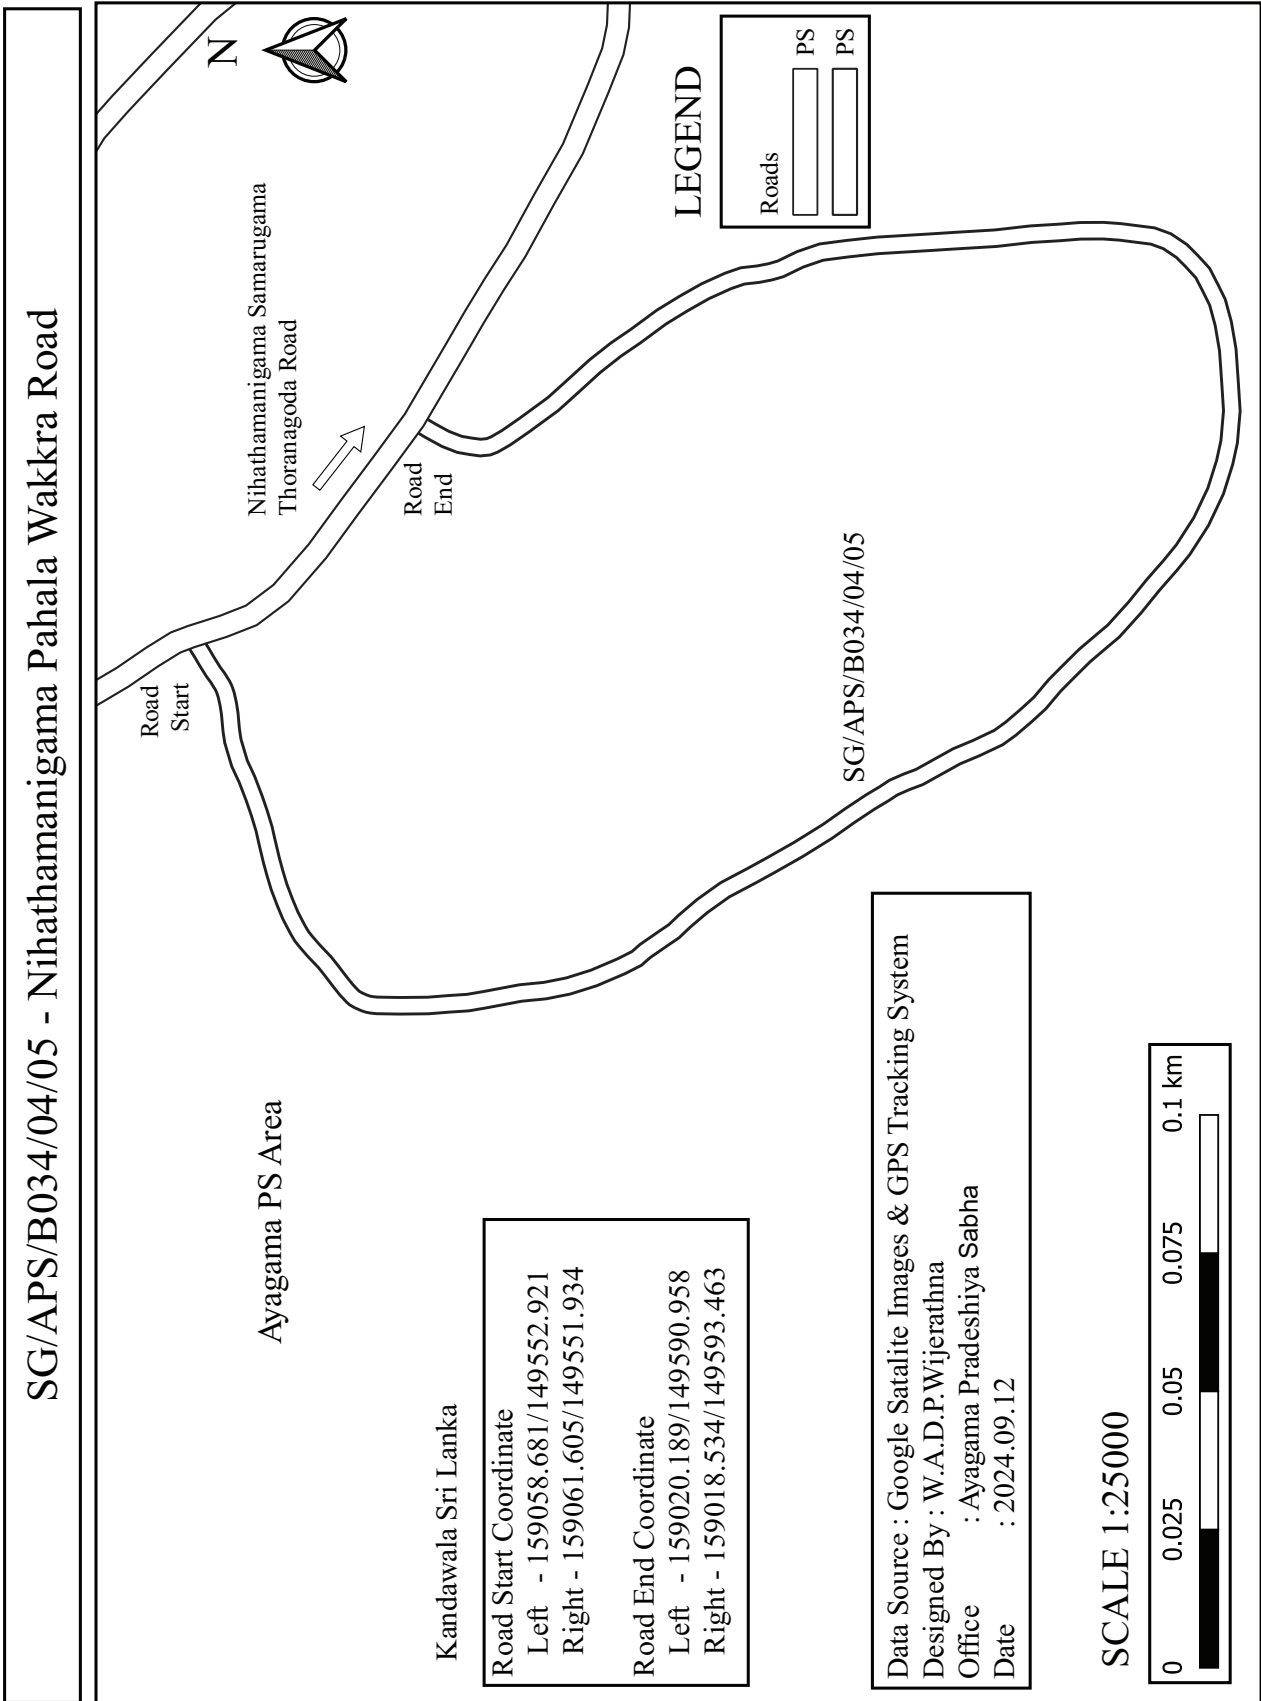


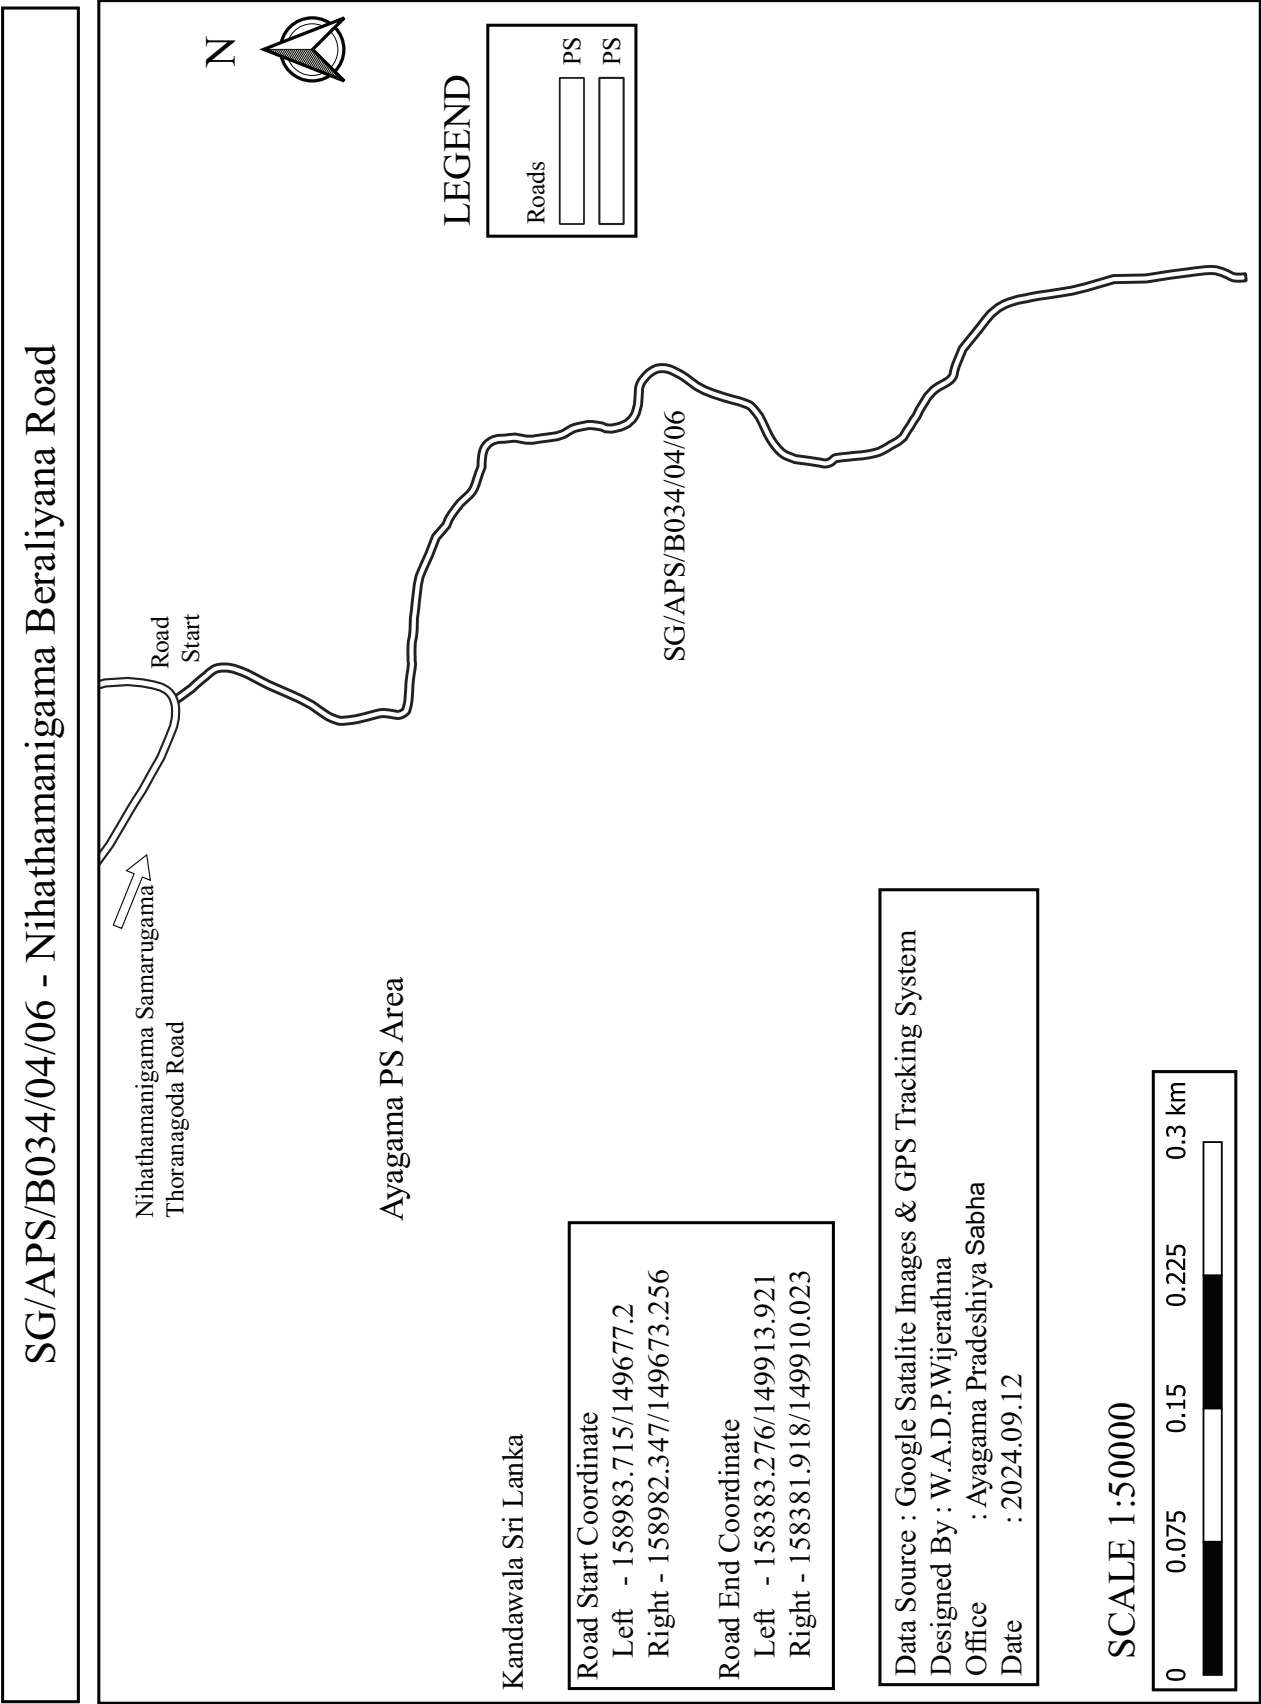


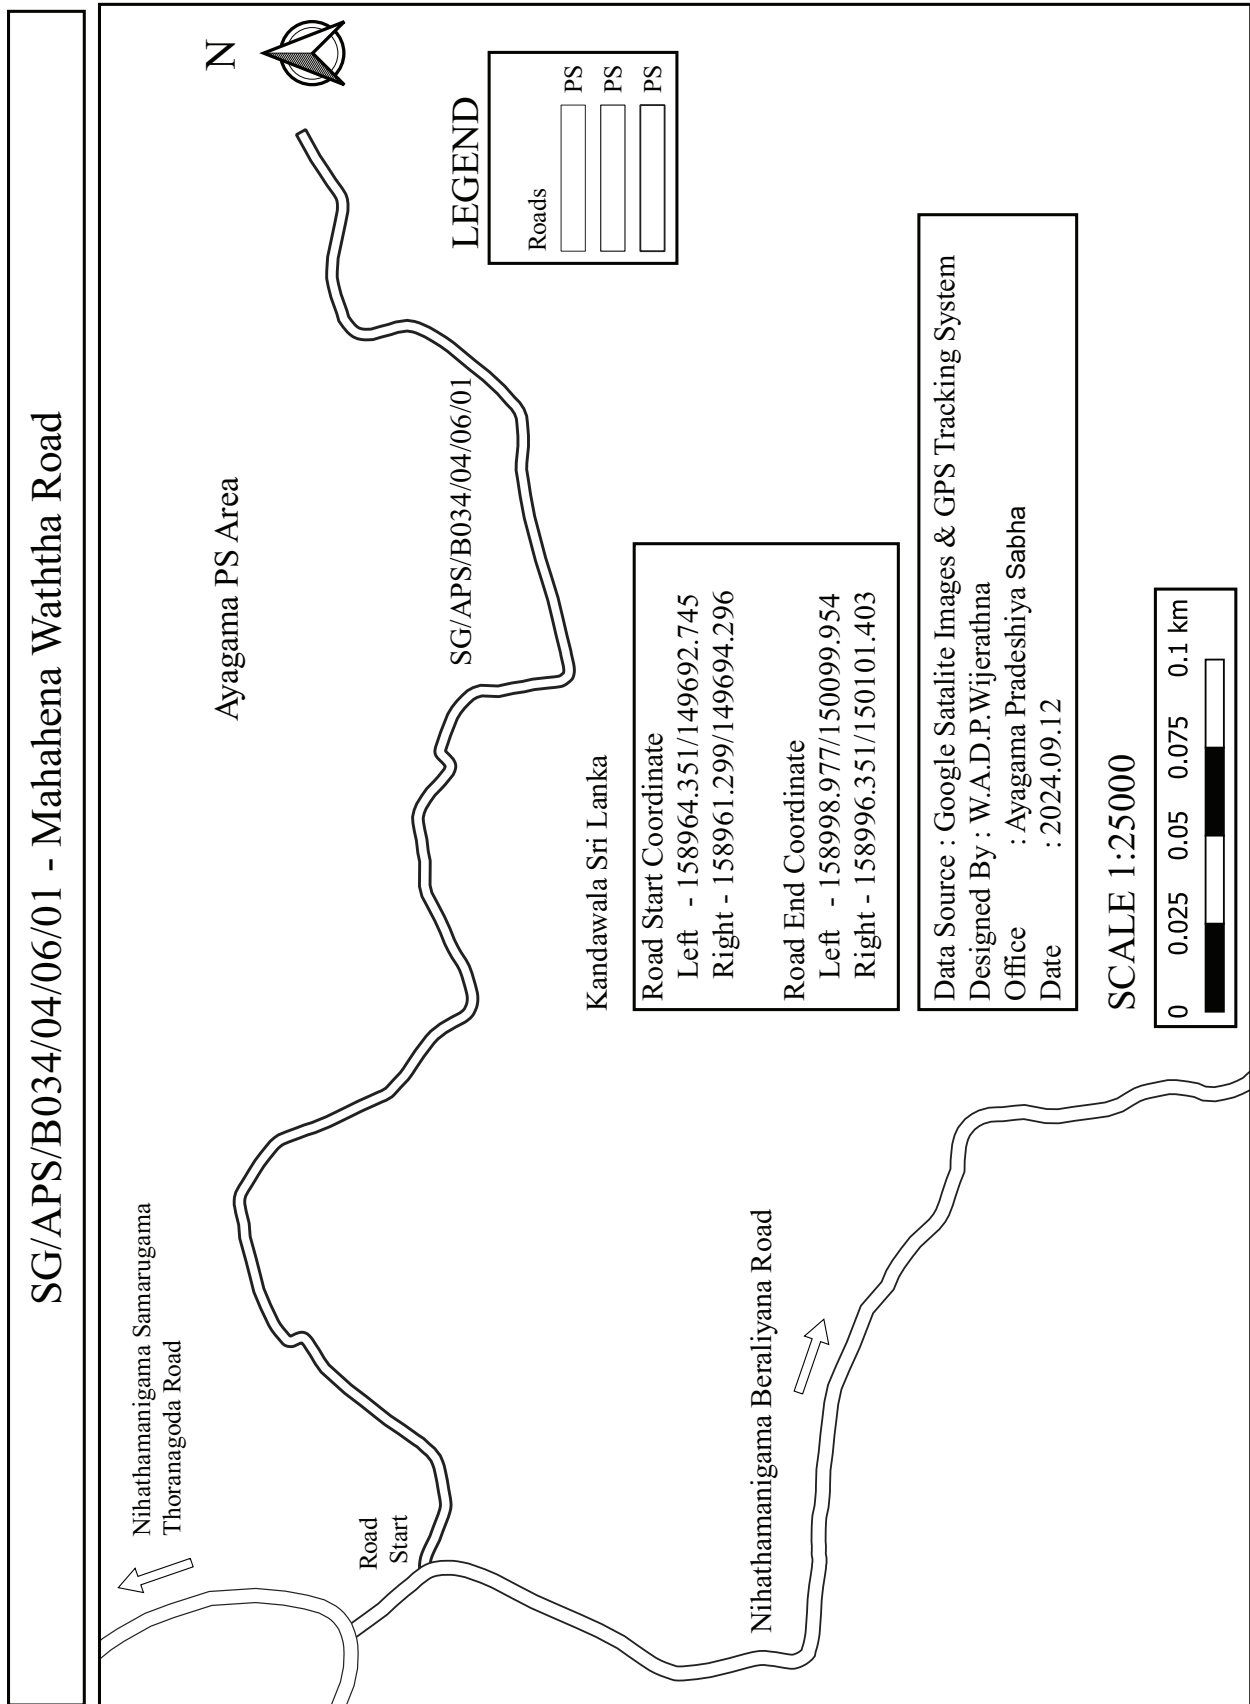


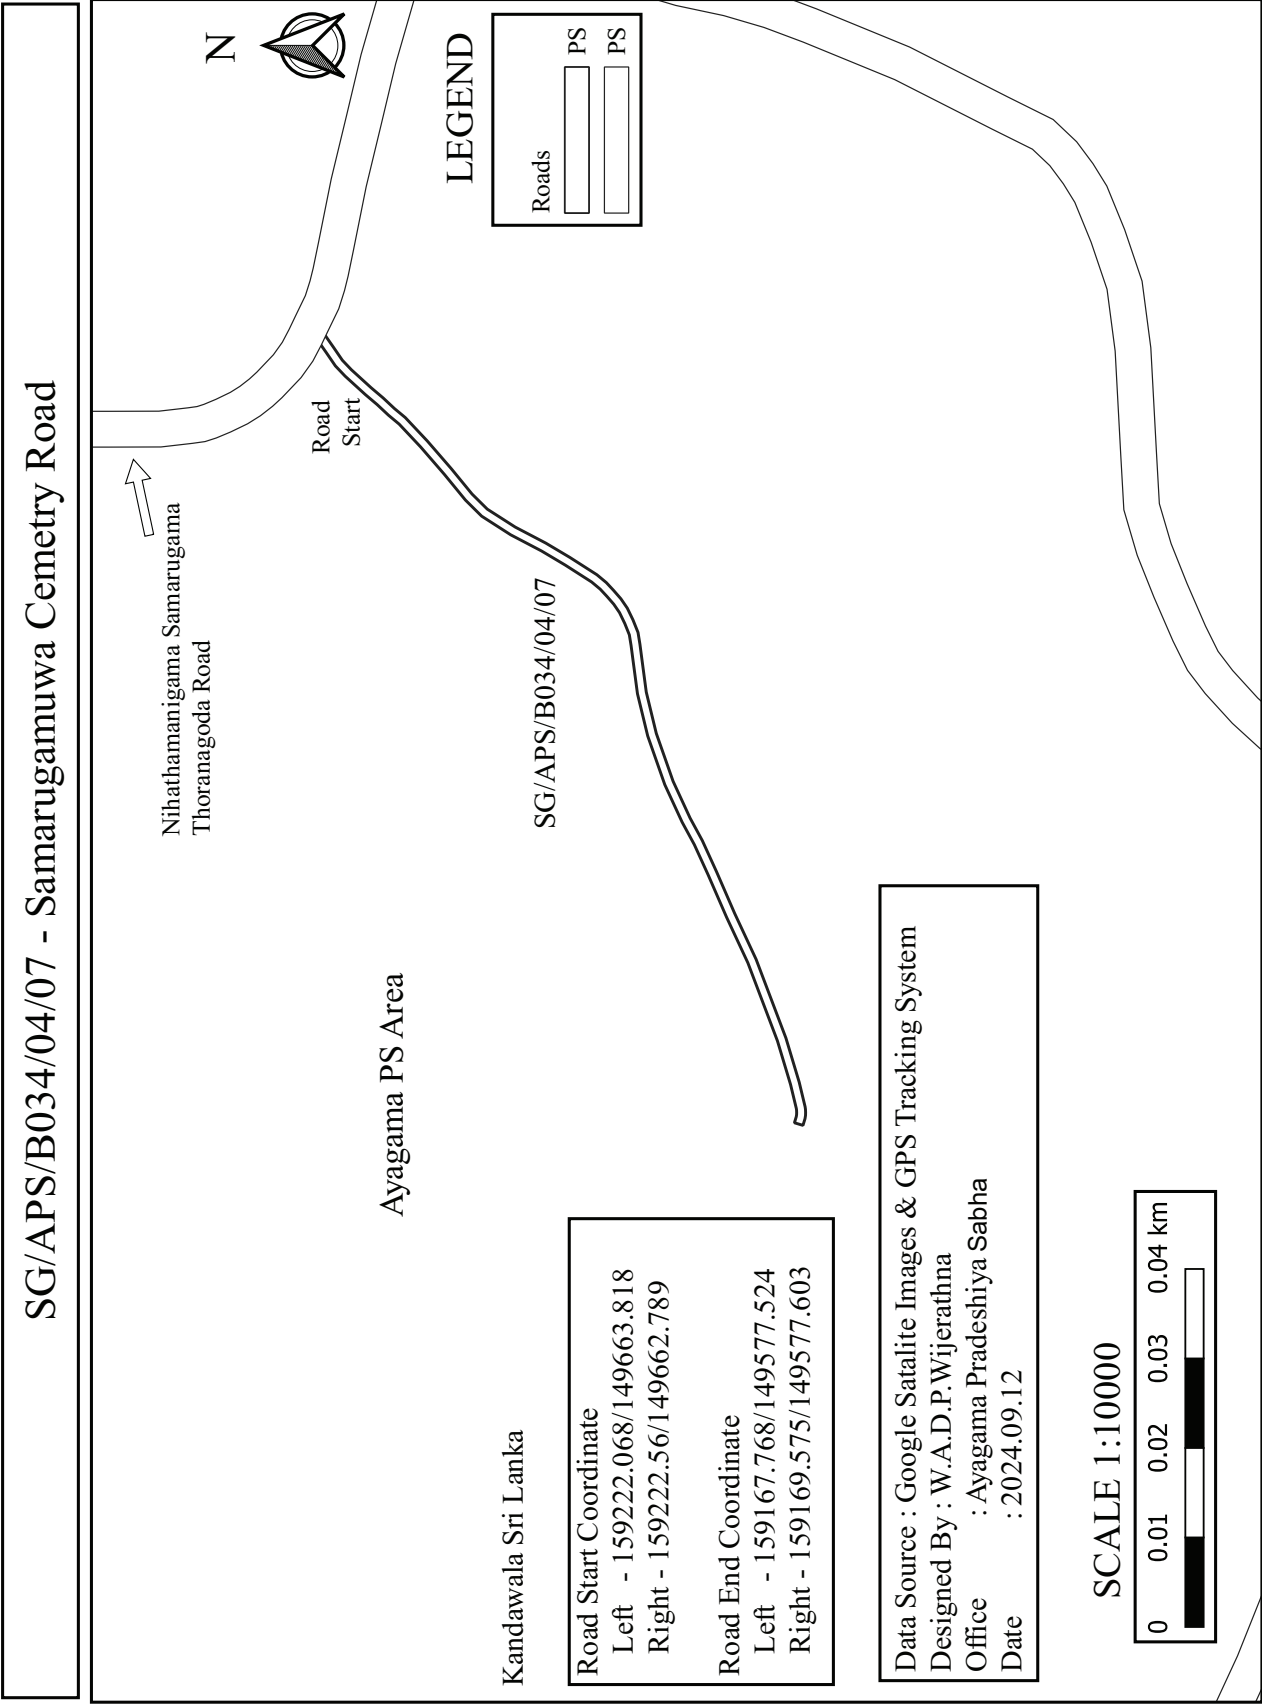

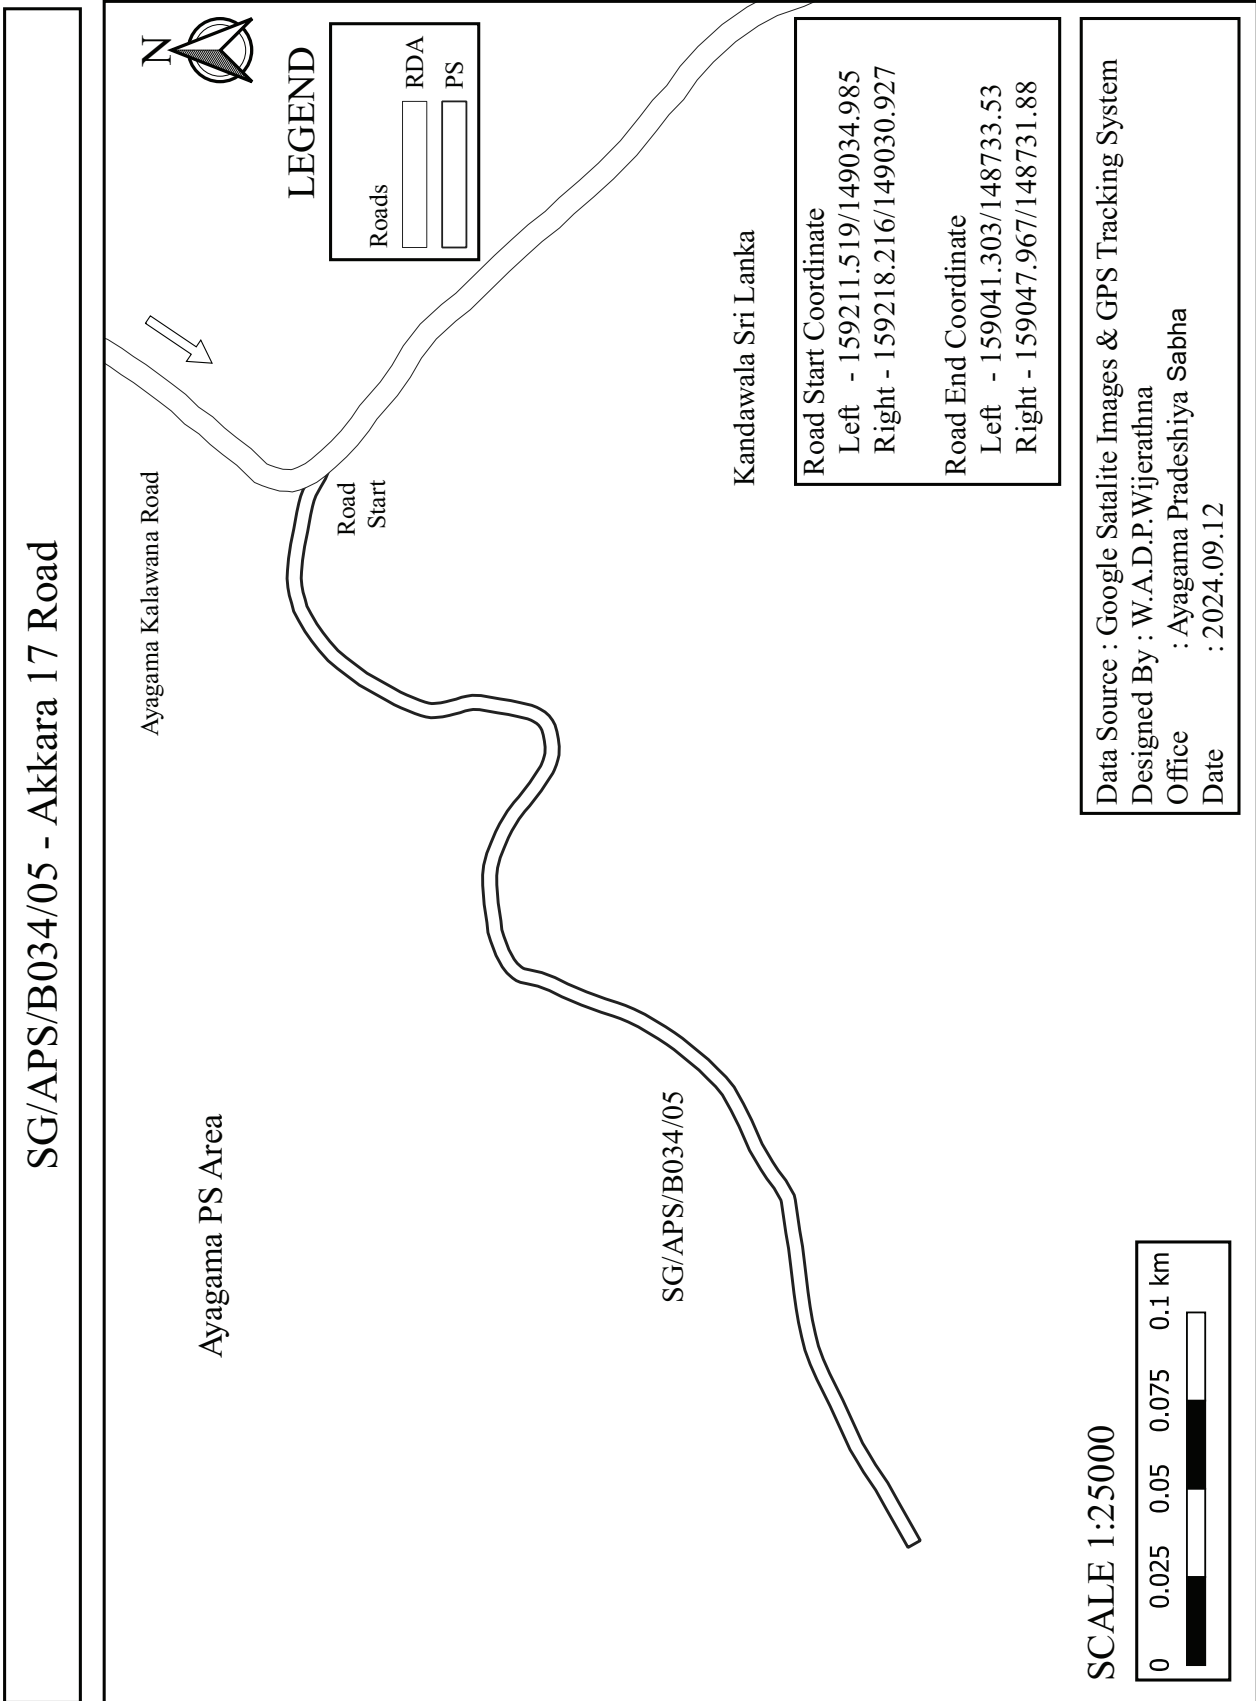


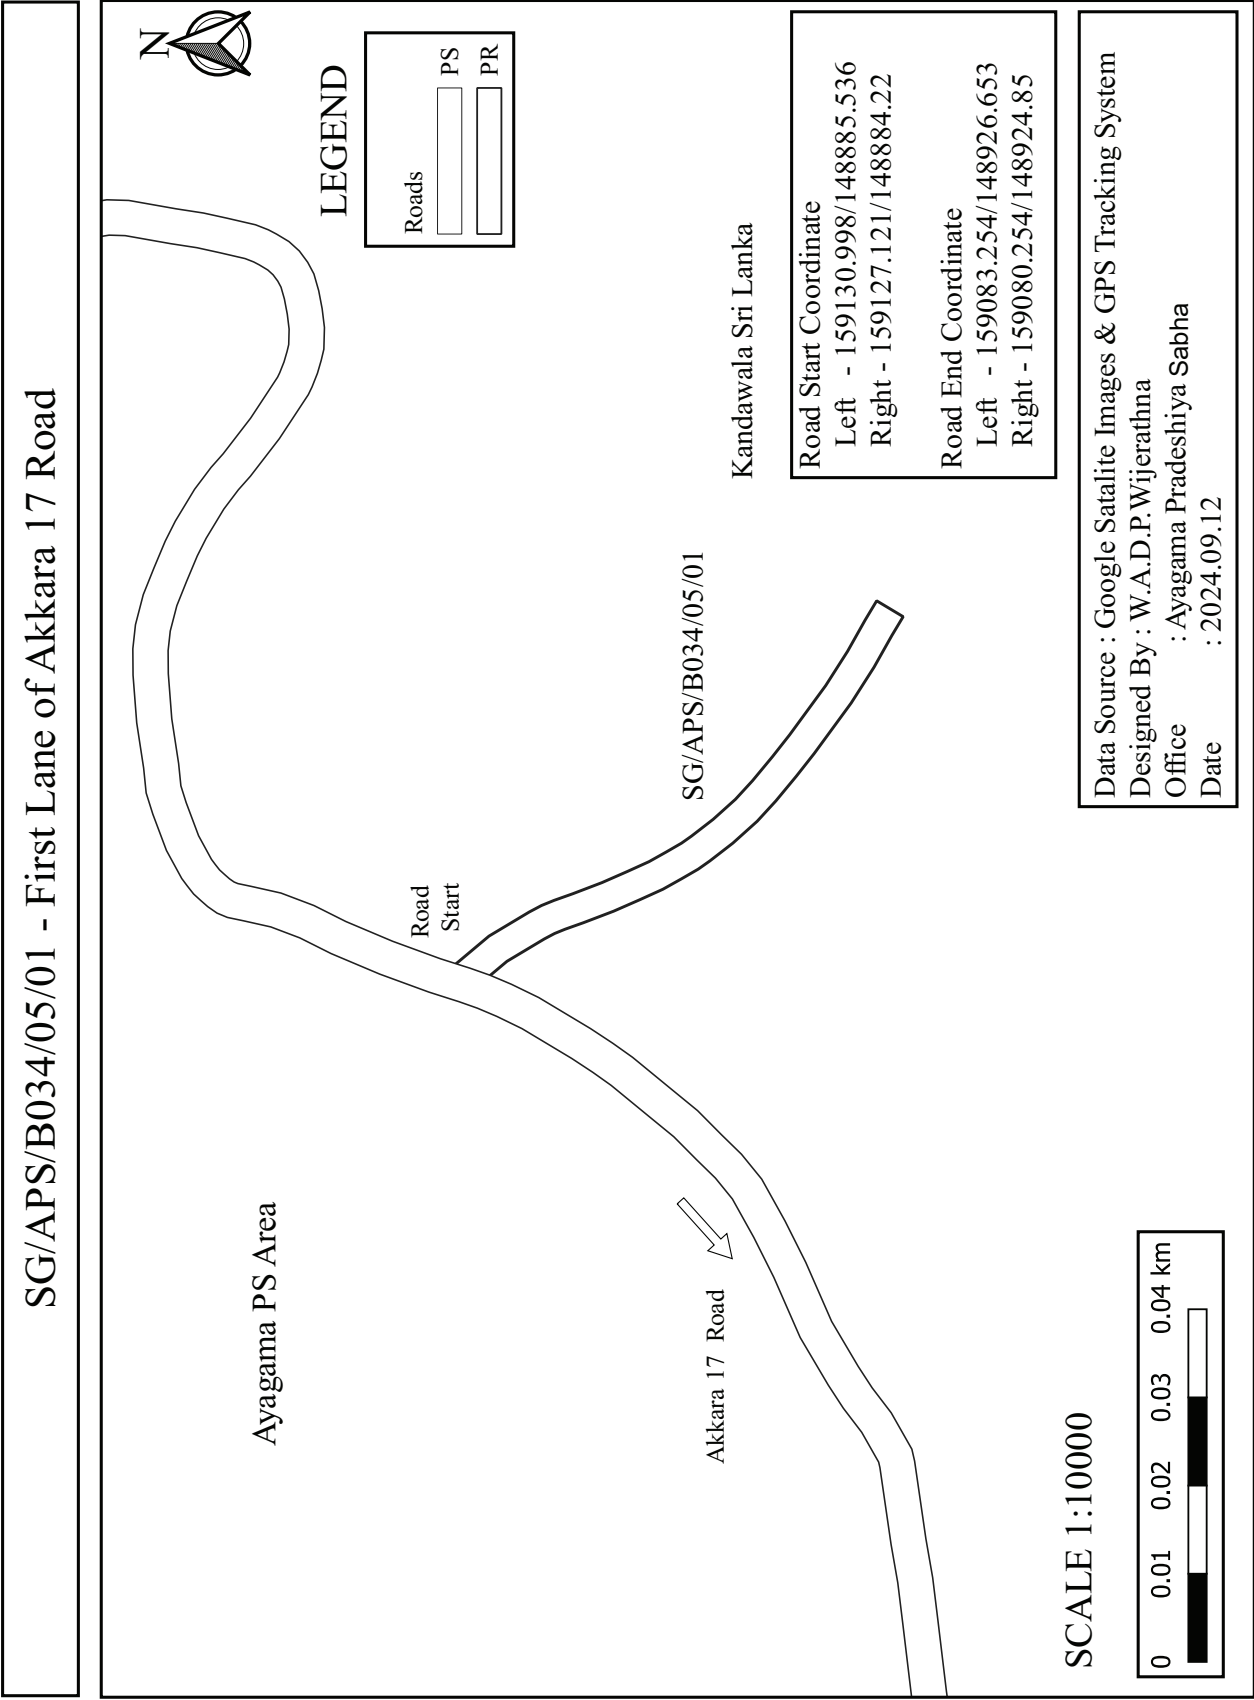


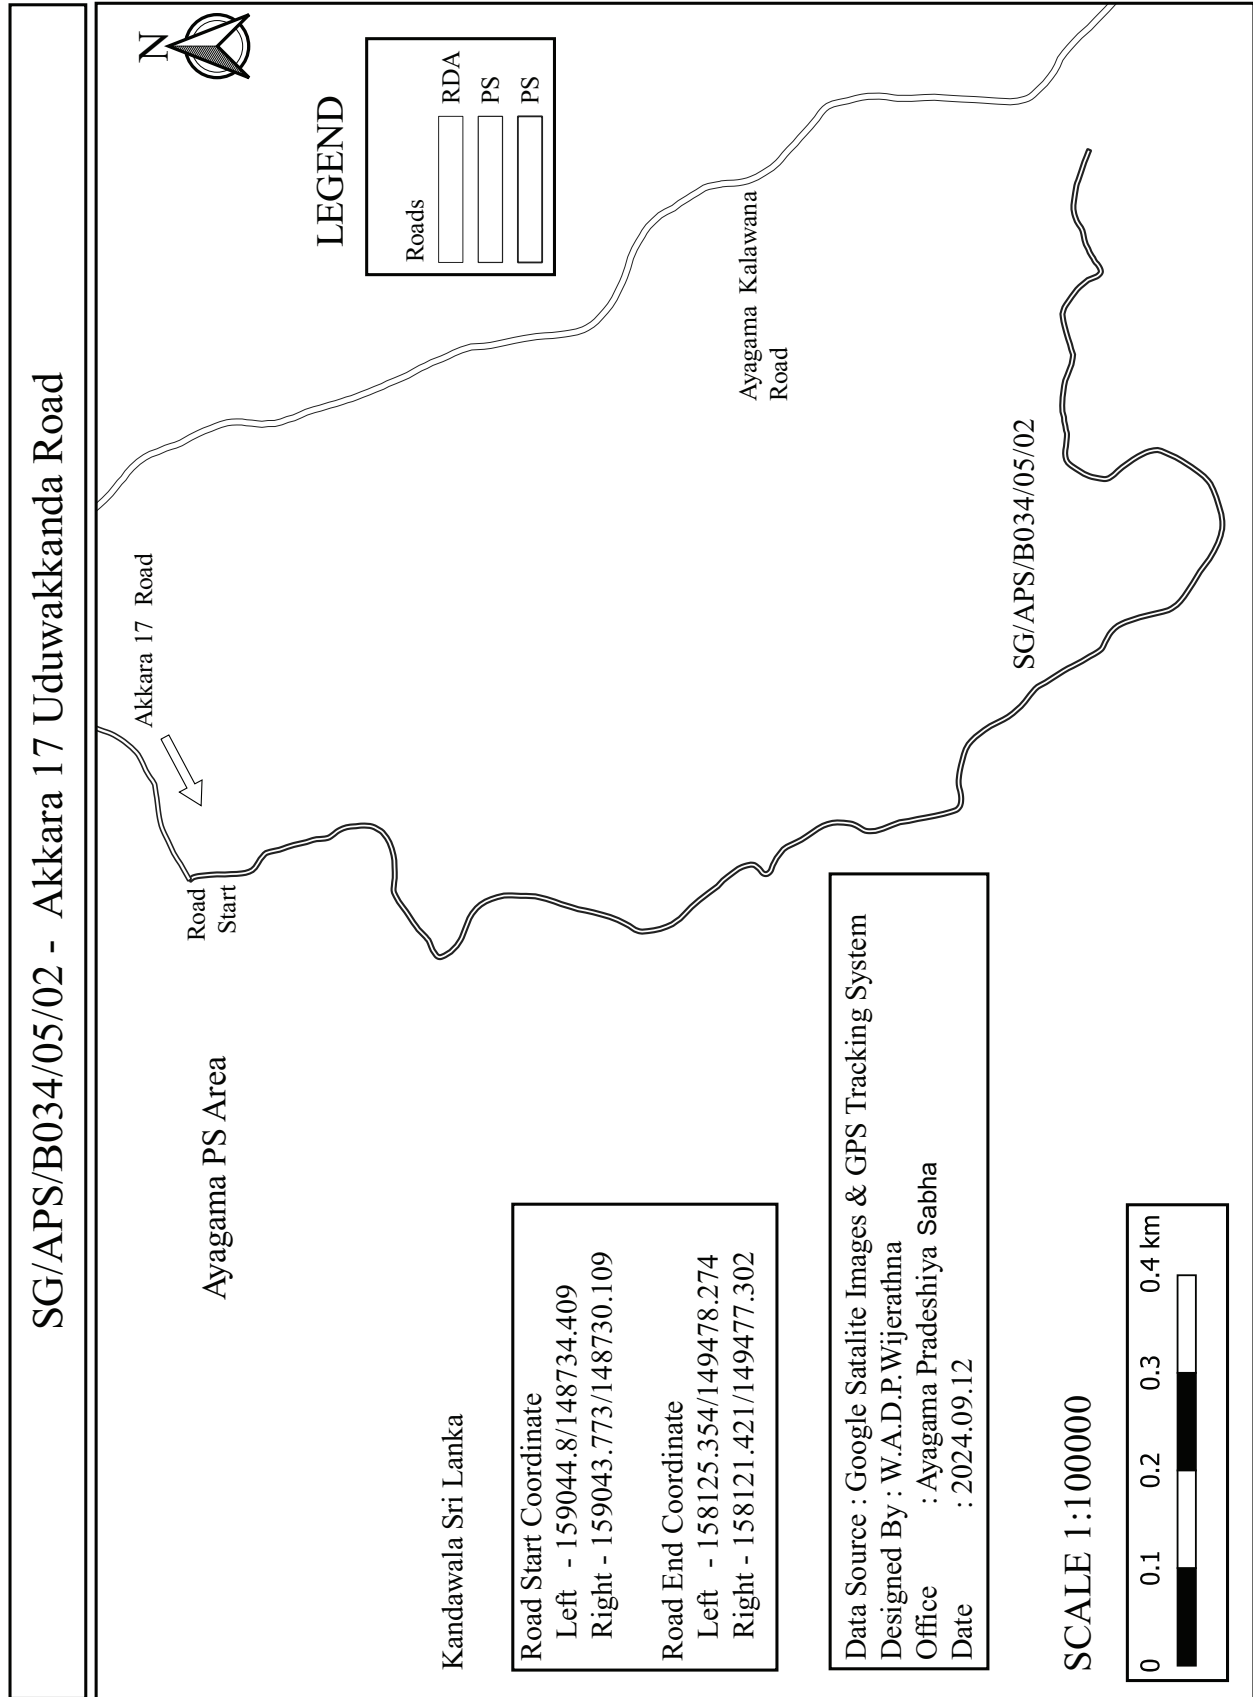

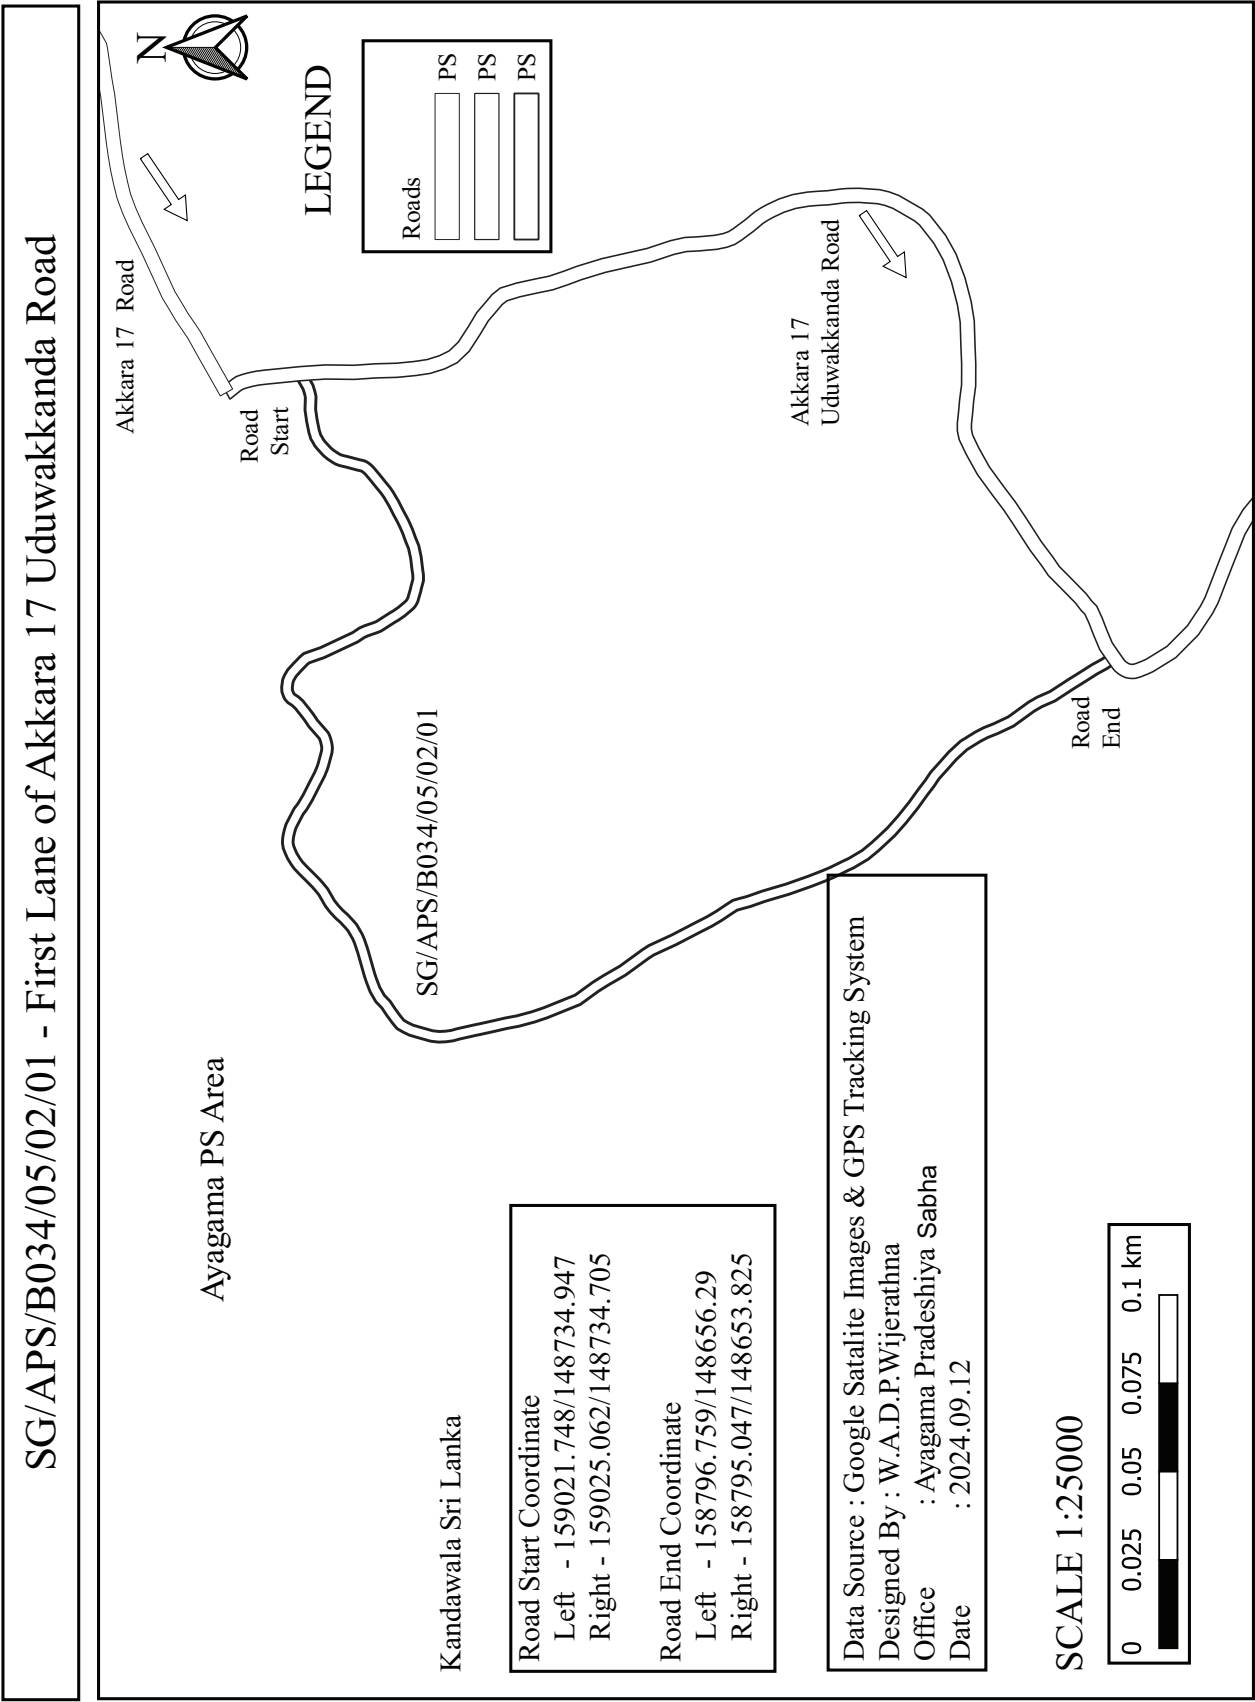



SG/APS/B034/05/02/01/01 - First By Pass of Akkara 17 Uduwakkanda Road

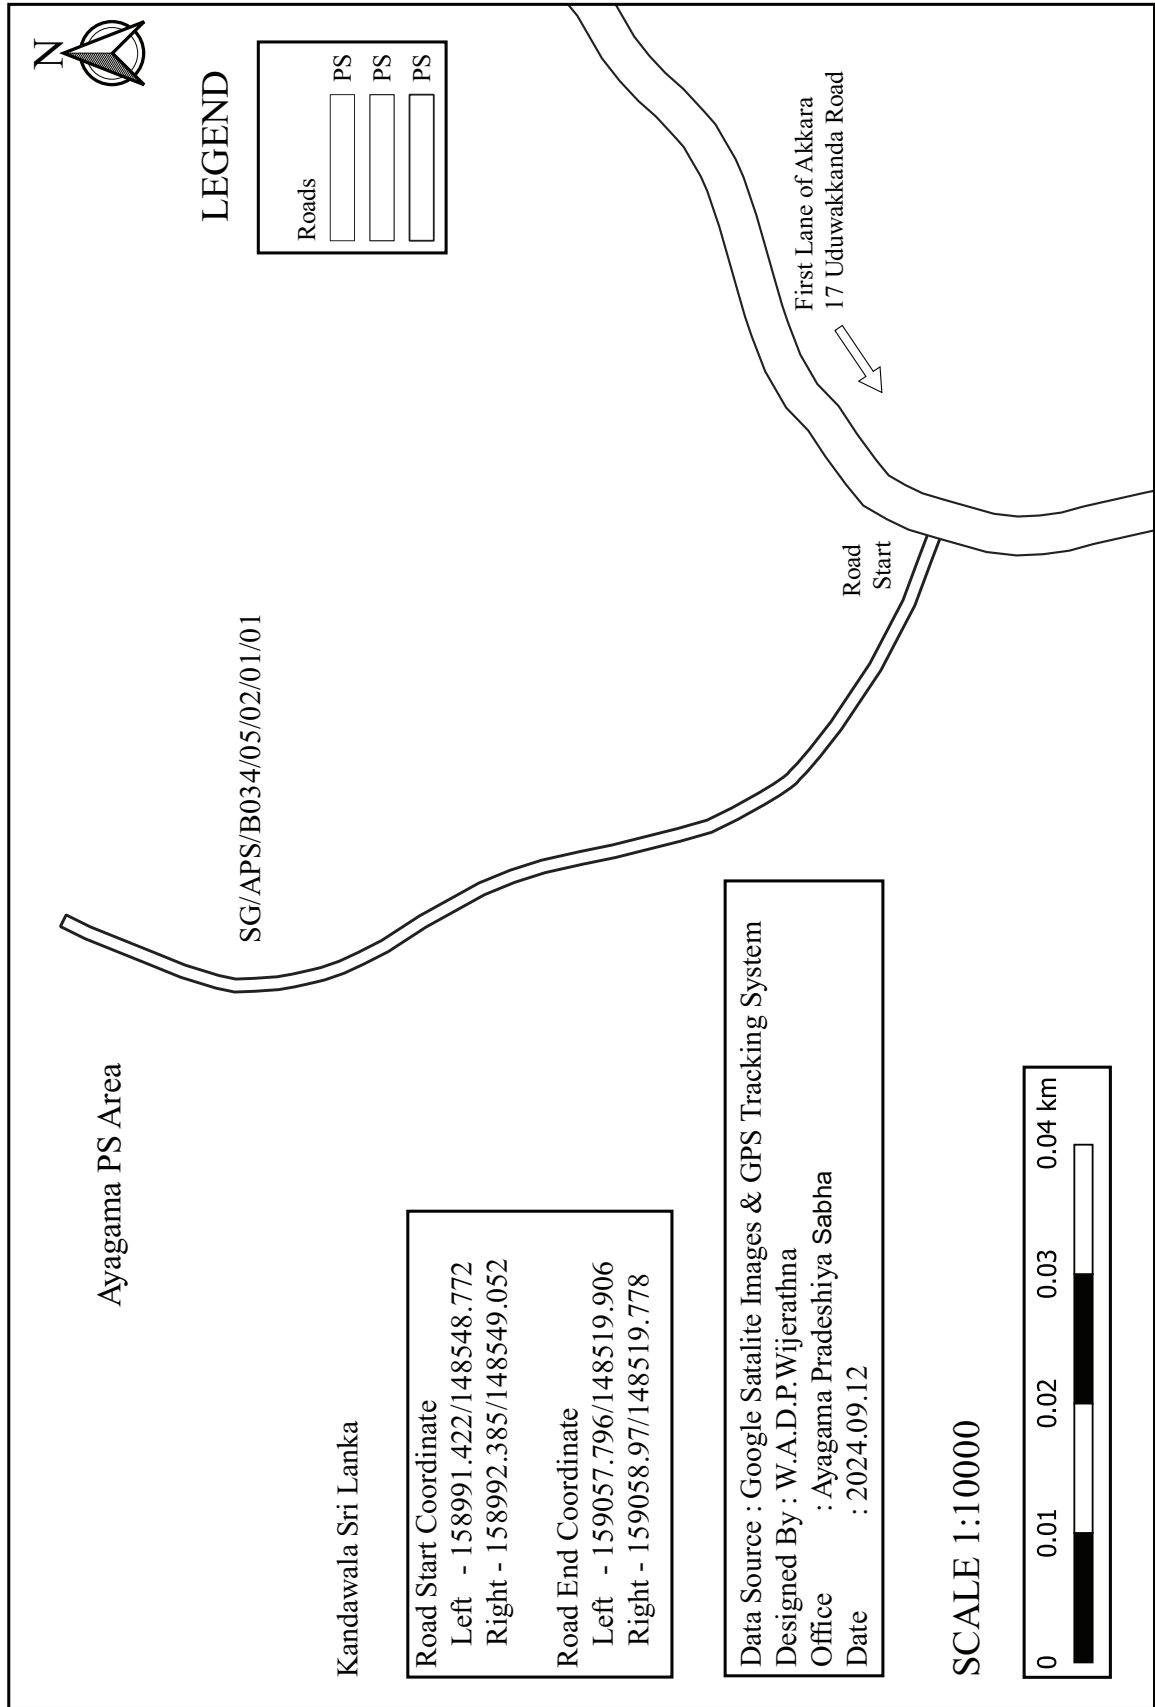

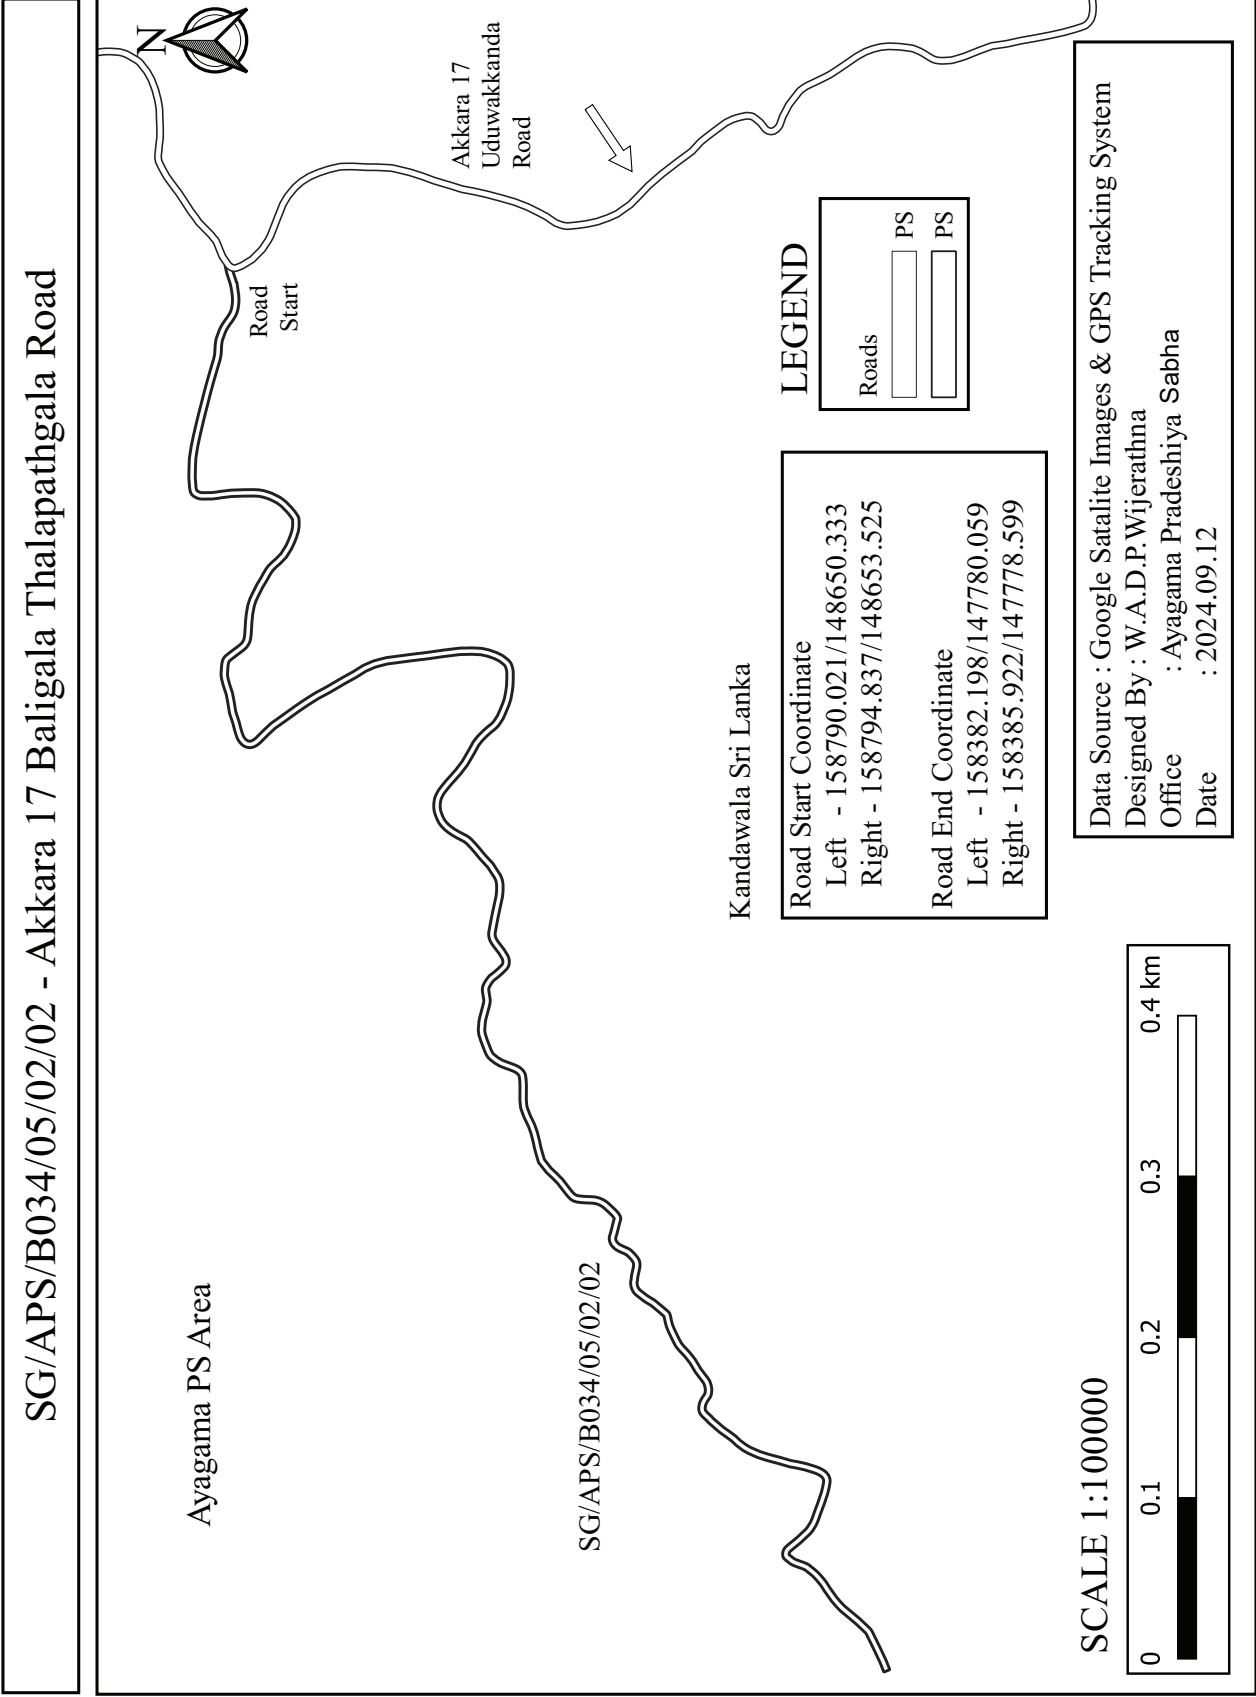



SG/APS/B034/05/02/02/01 - First Lane of Akkara 17 Baligala Thalapathgala Road

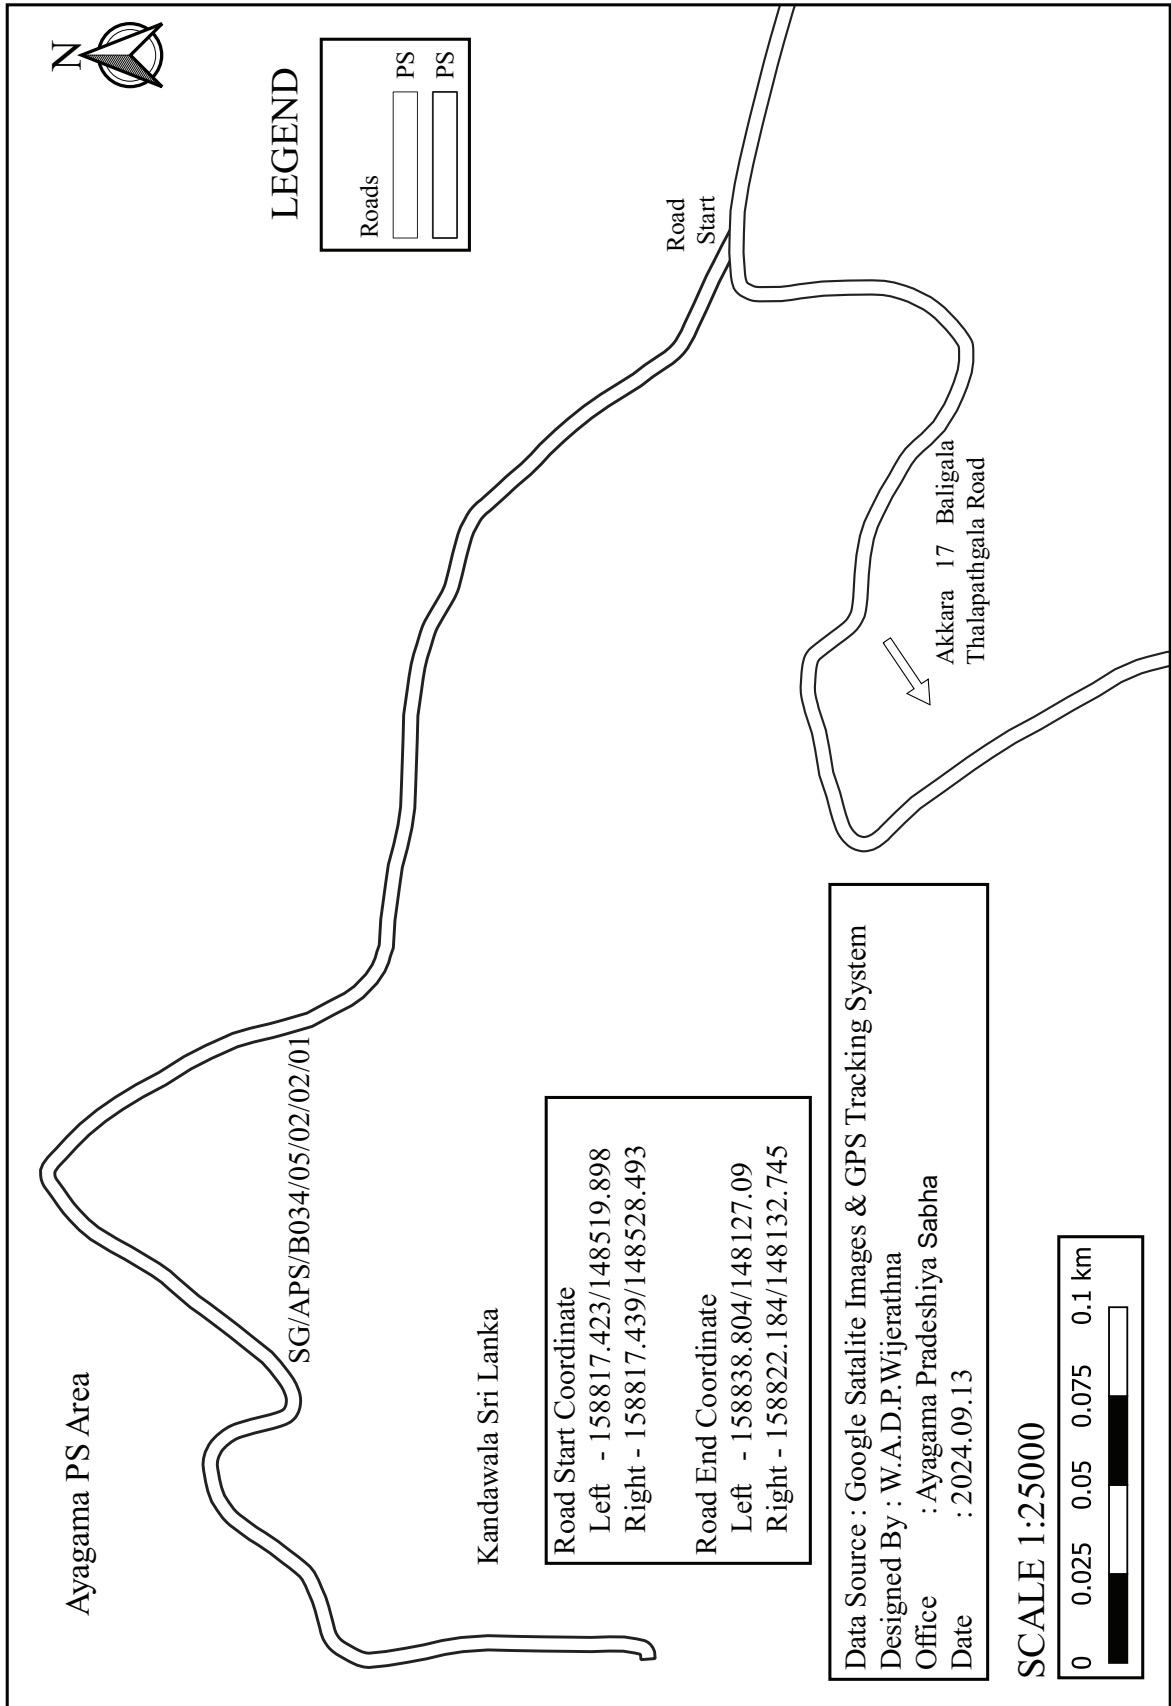


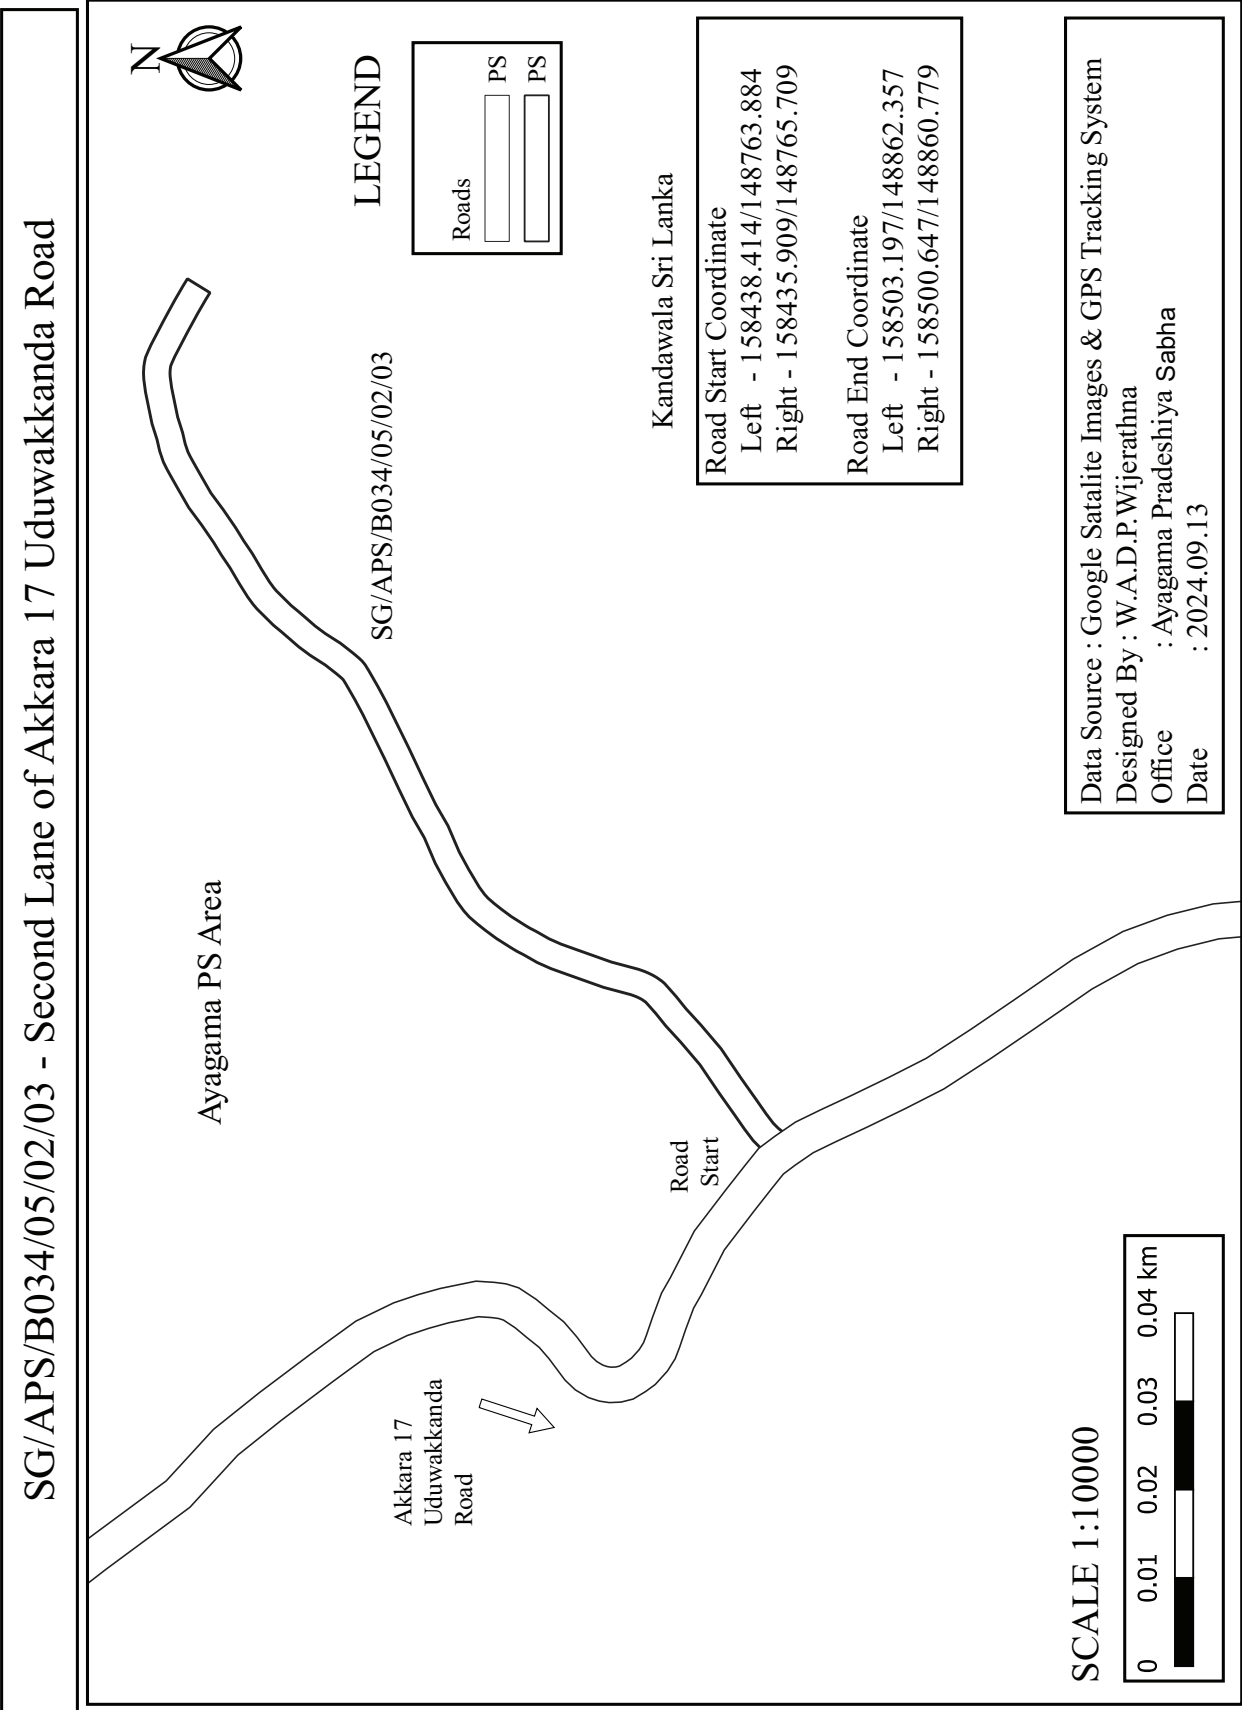



SG/APS/B034/06 -Ereporuwa First Lane

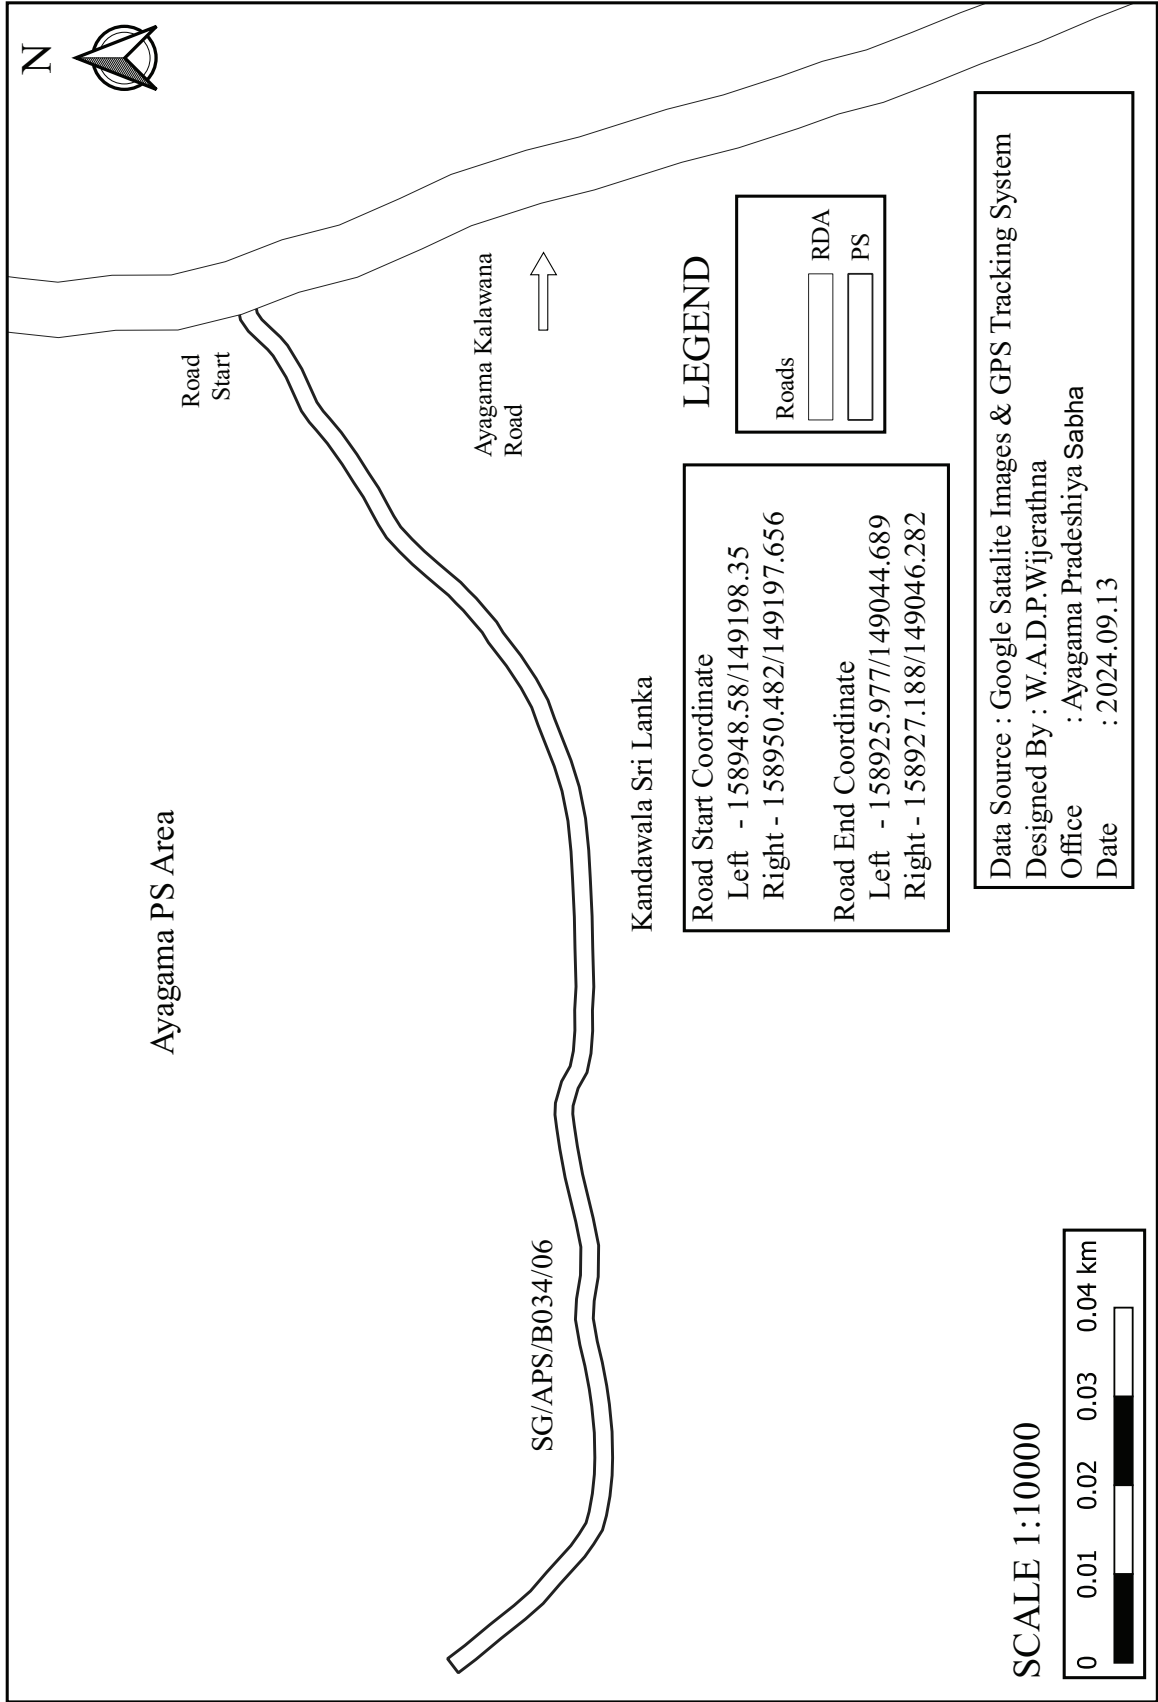


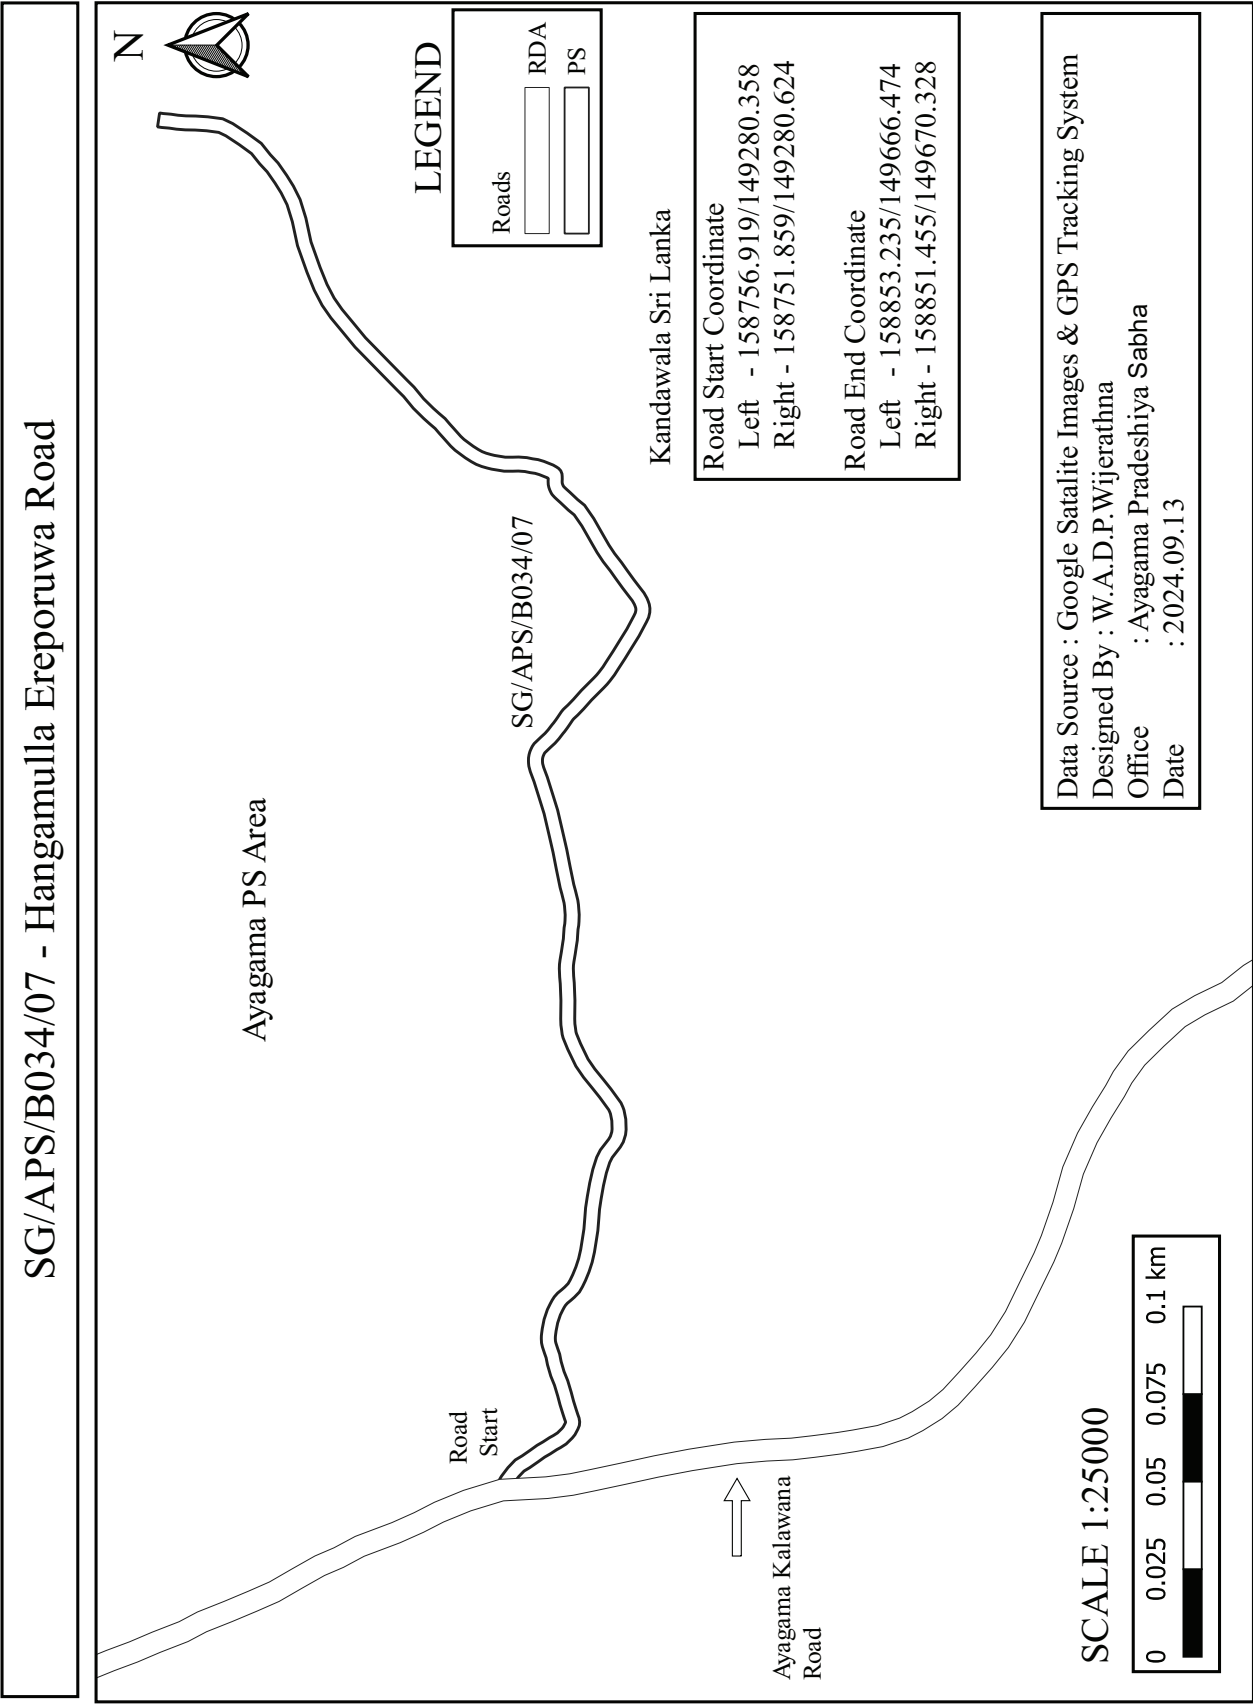


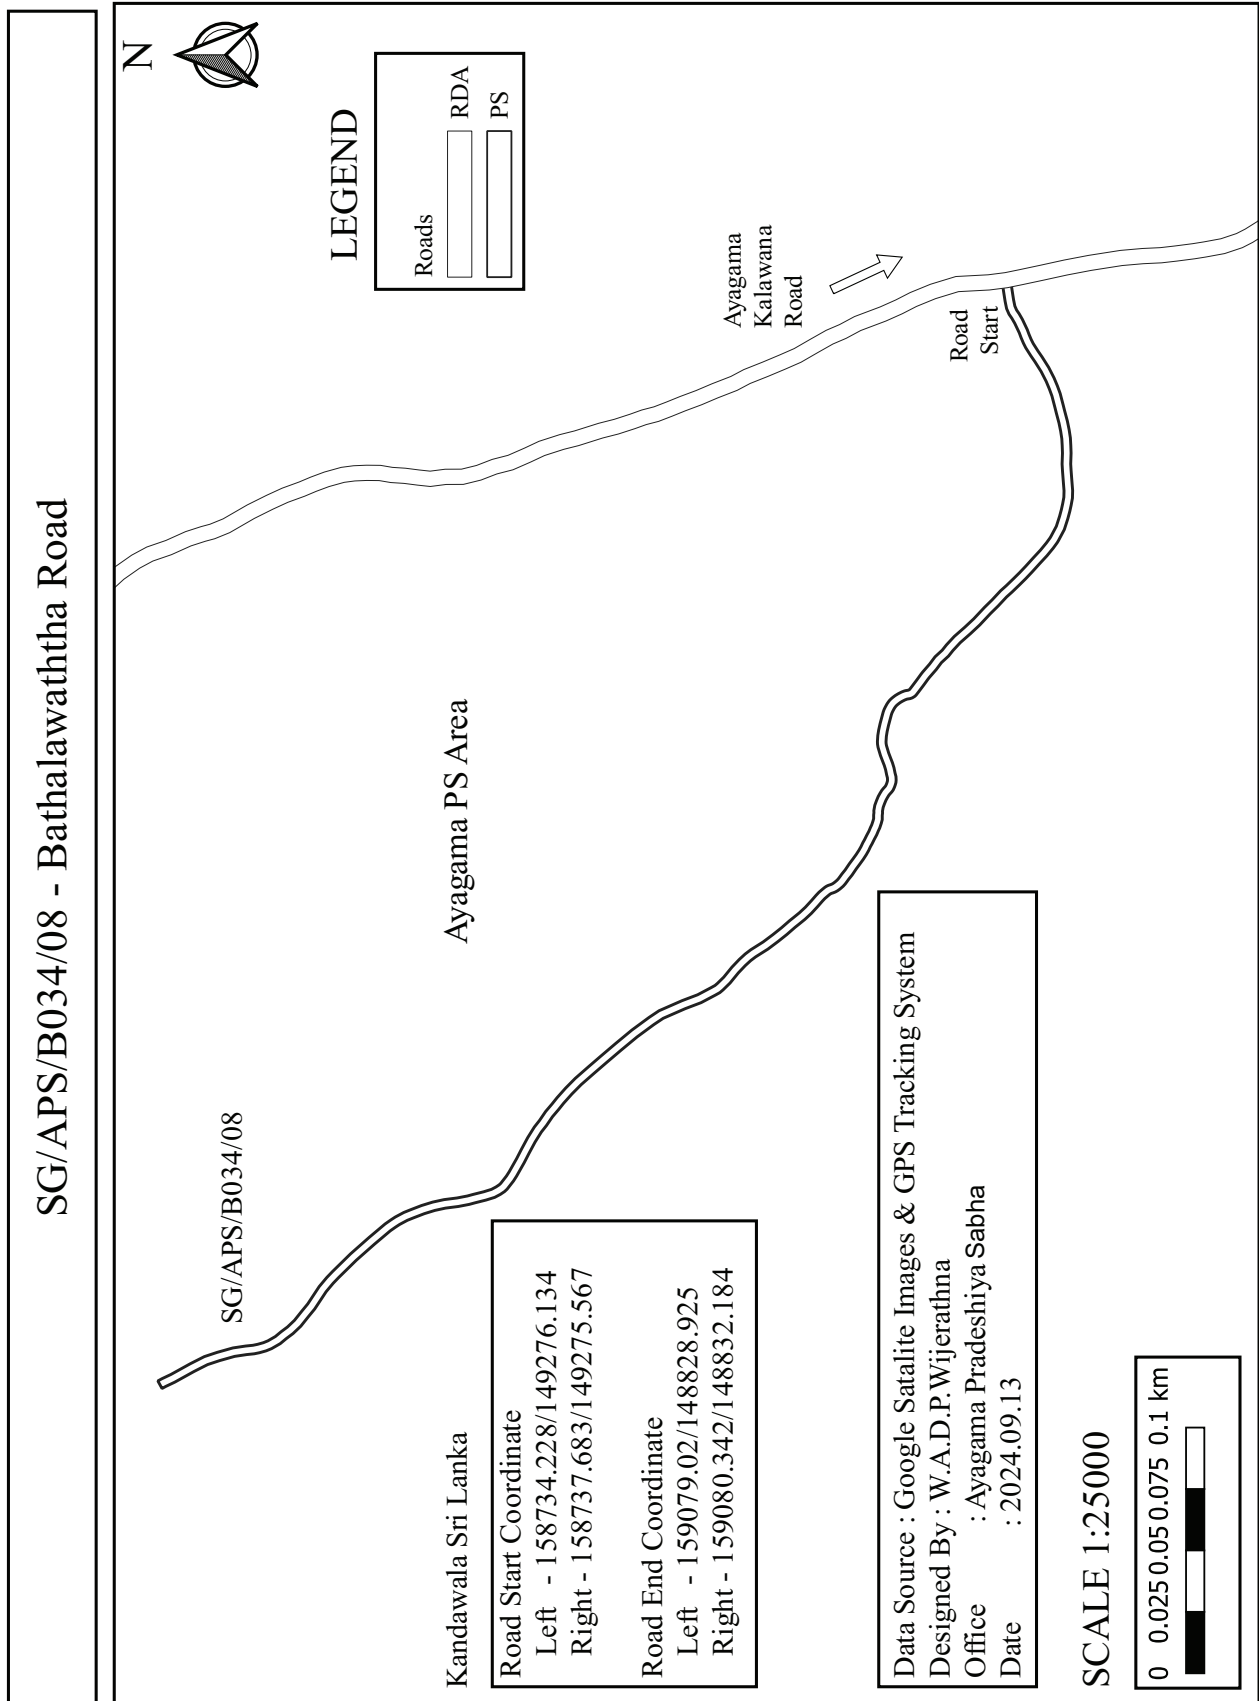


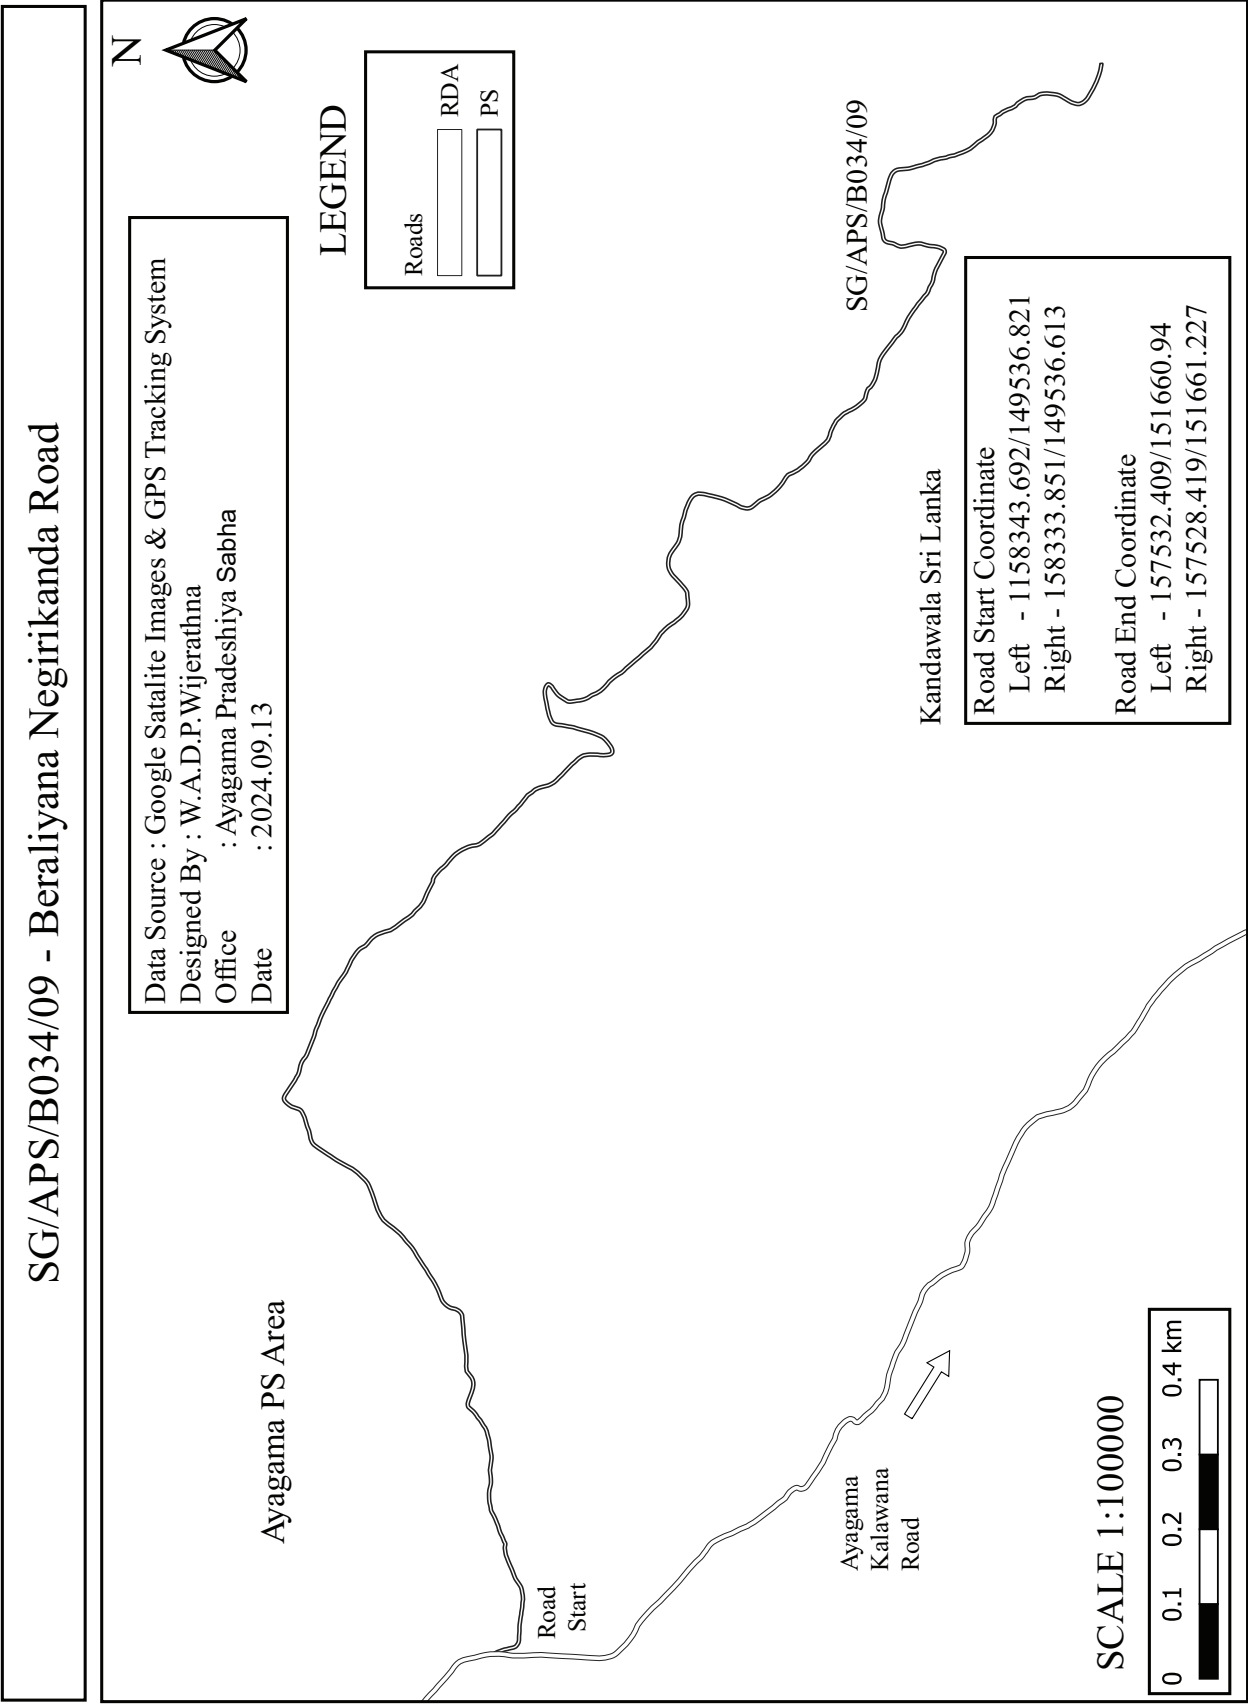


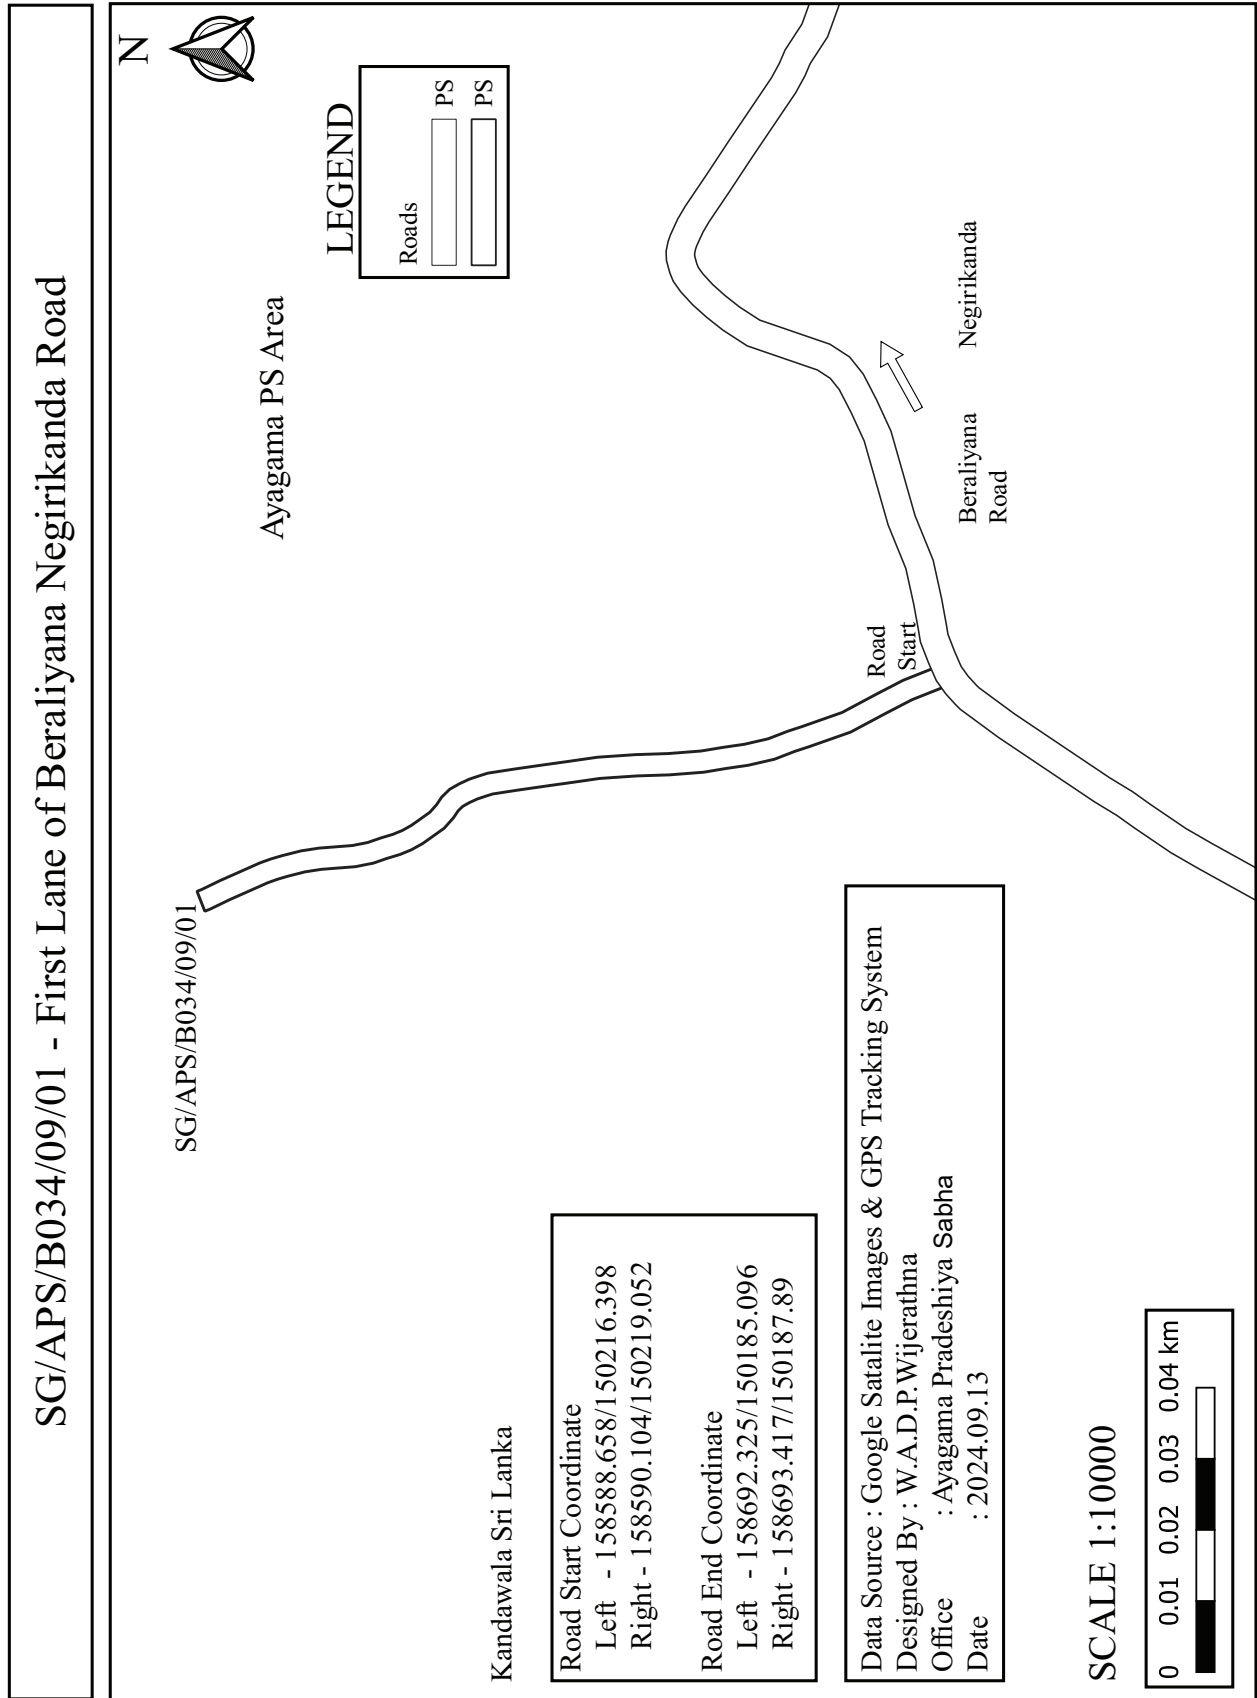


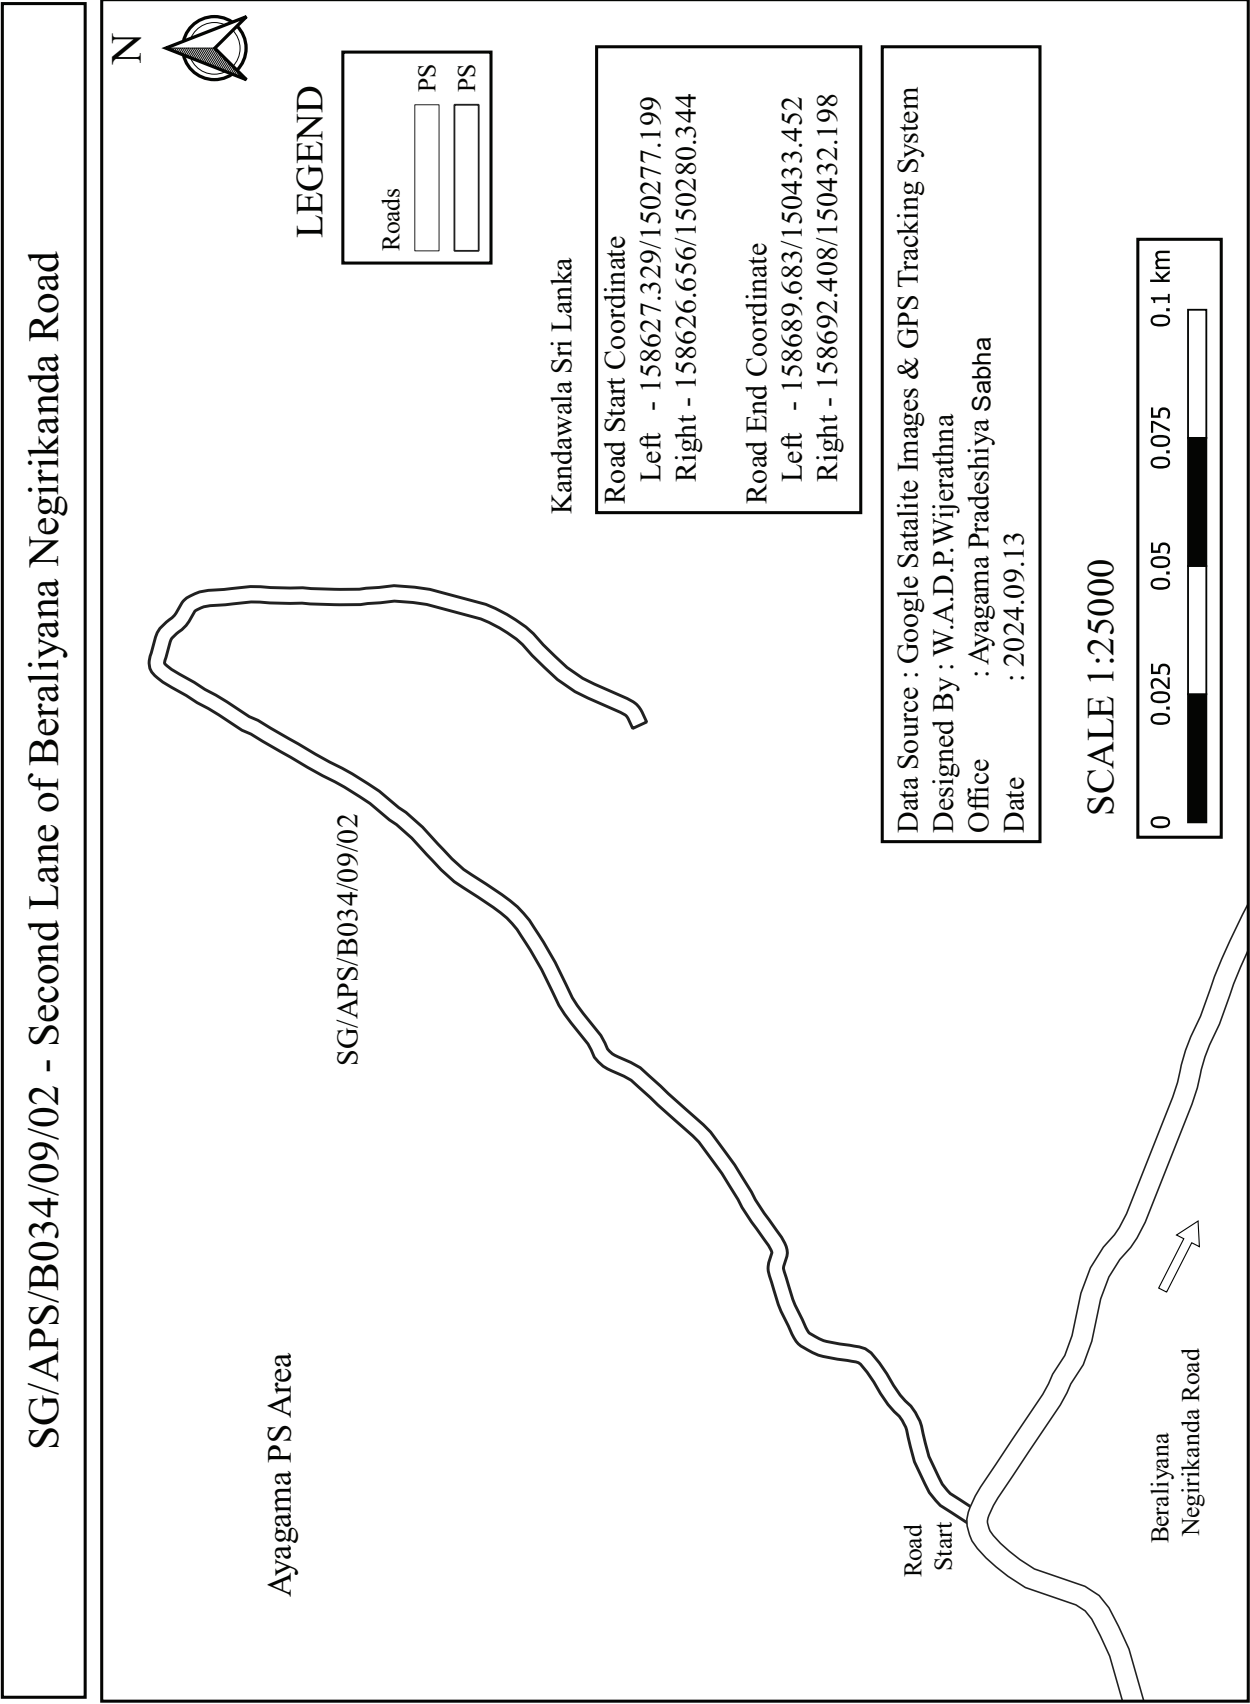


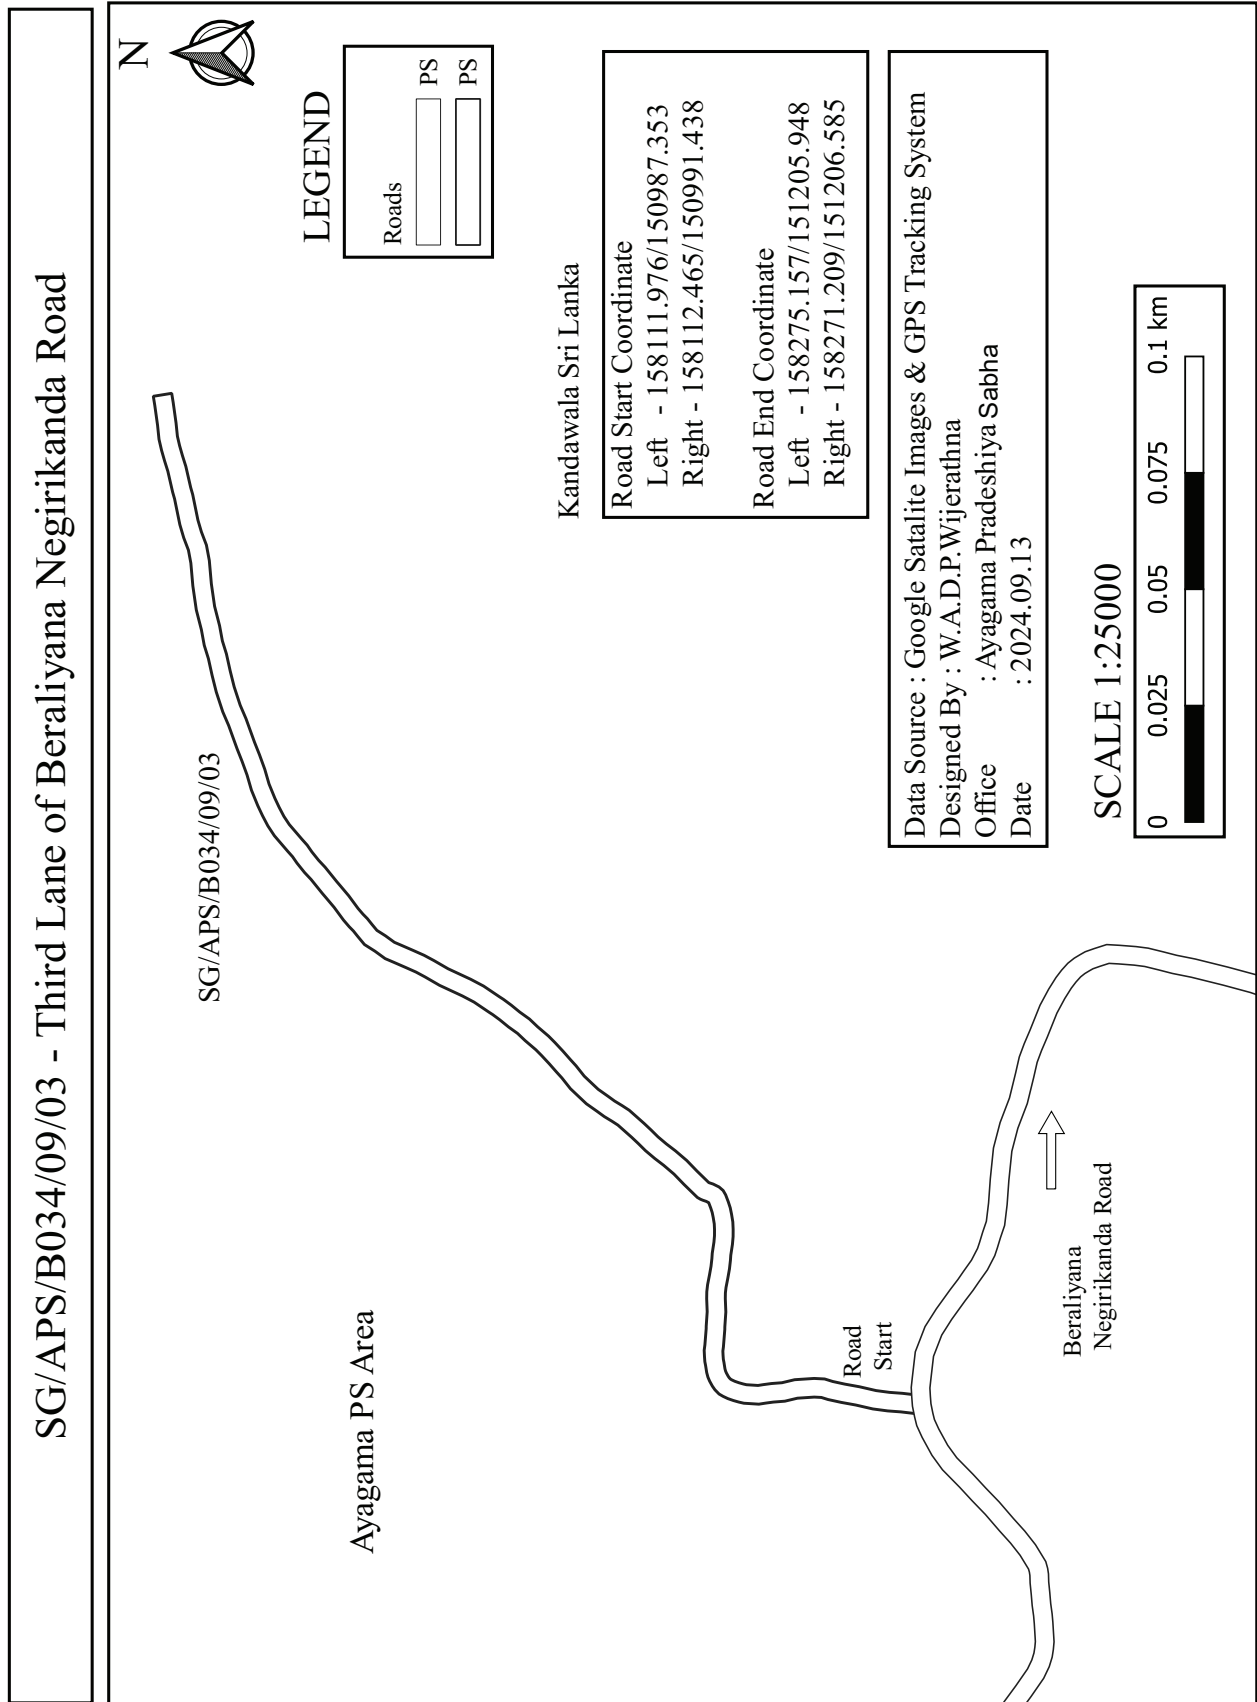


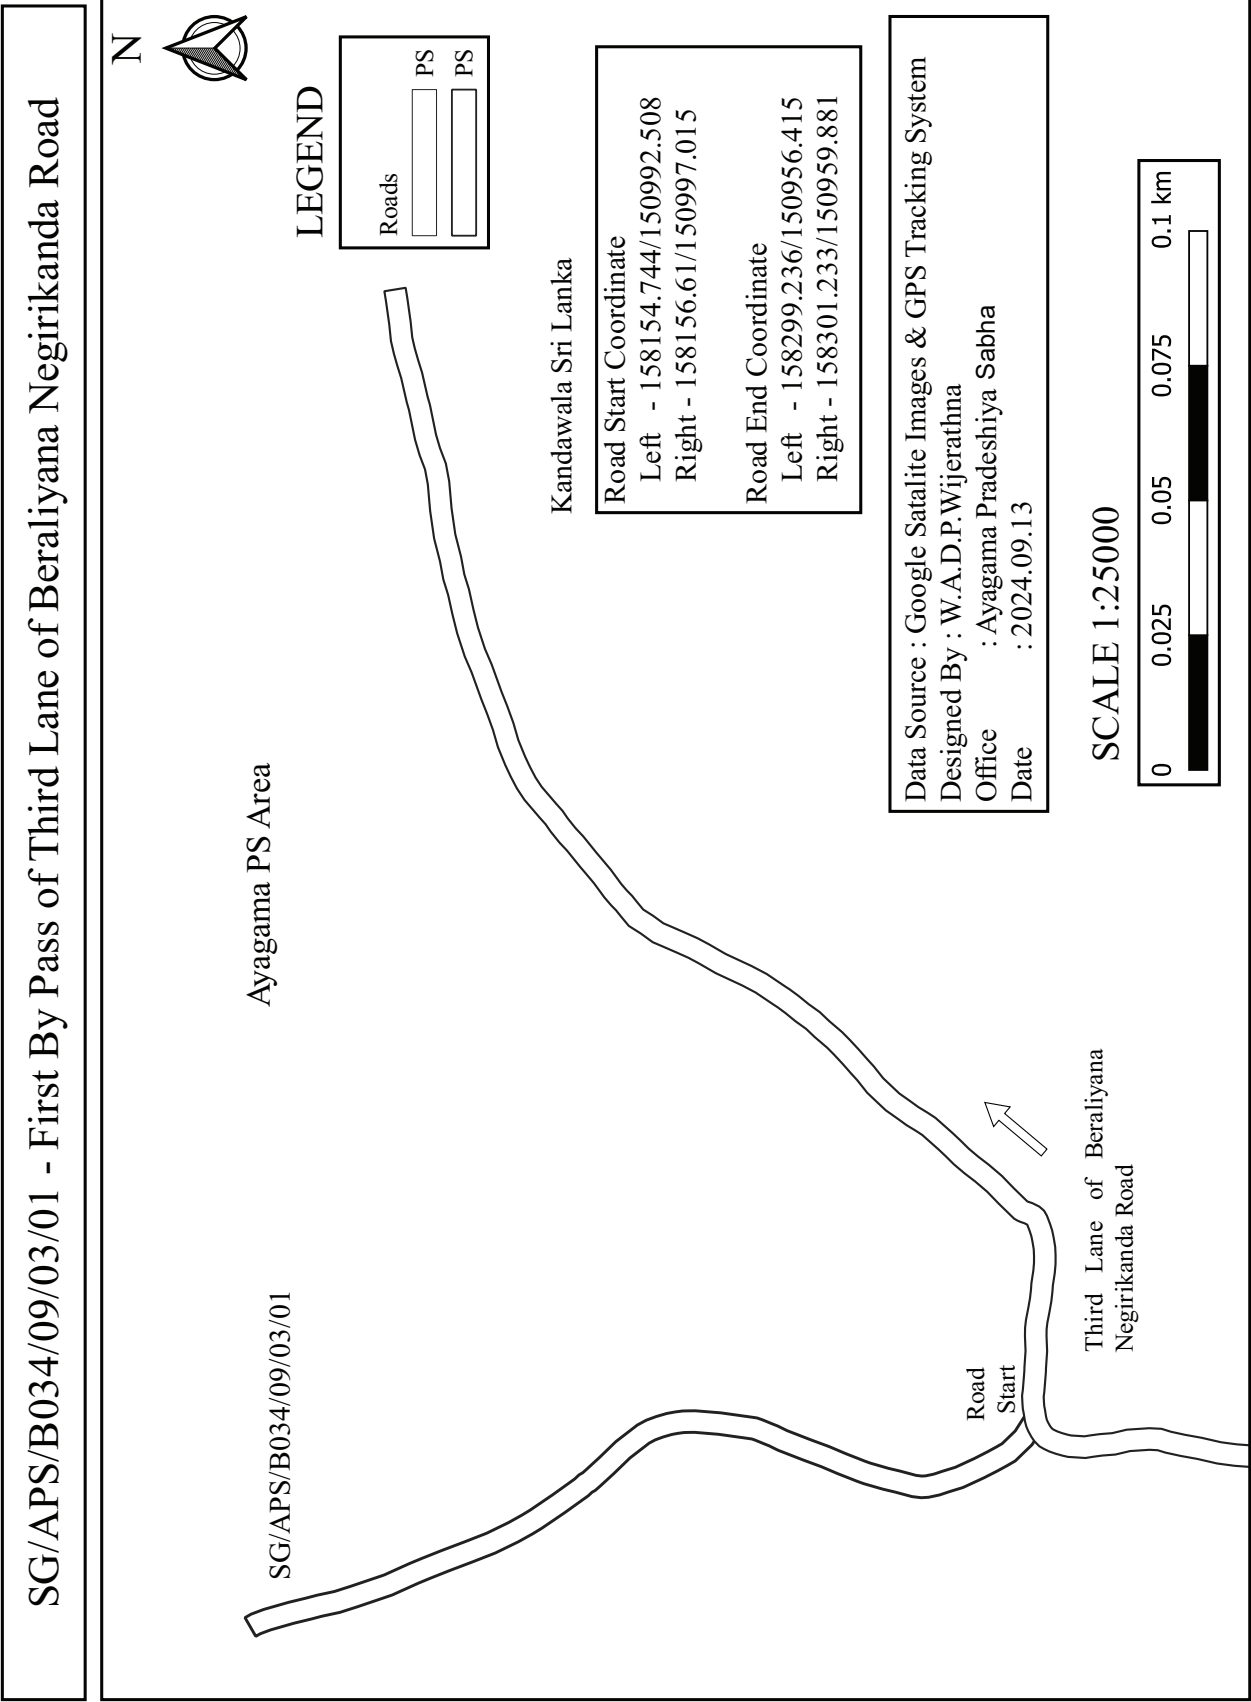


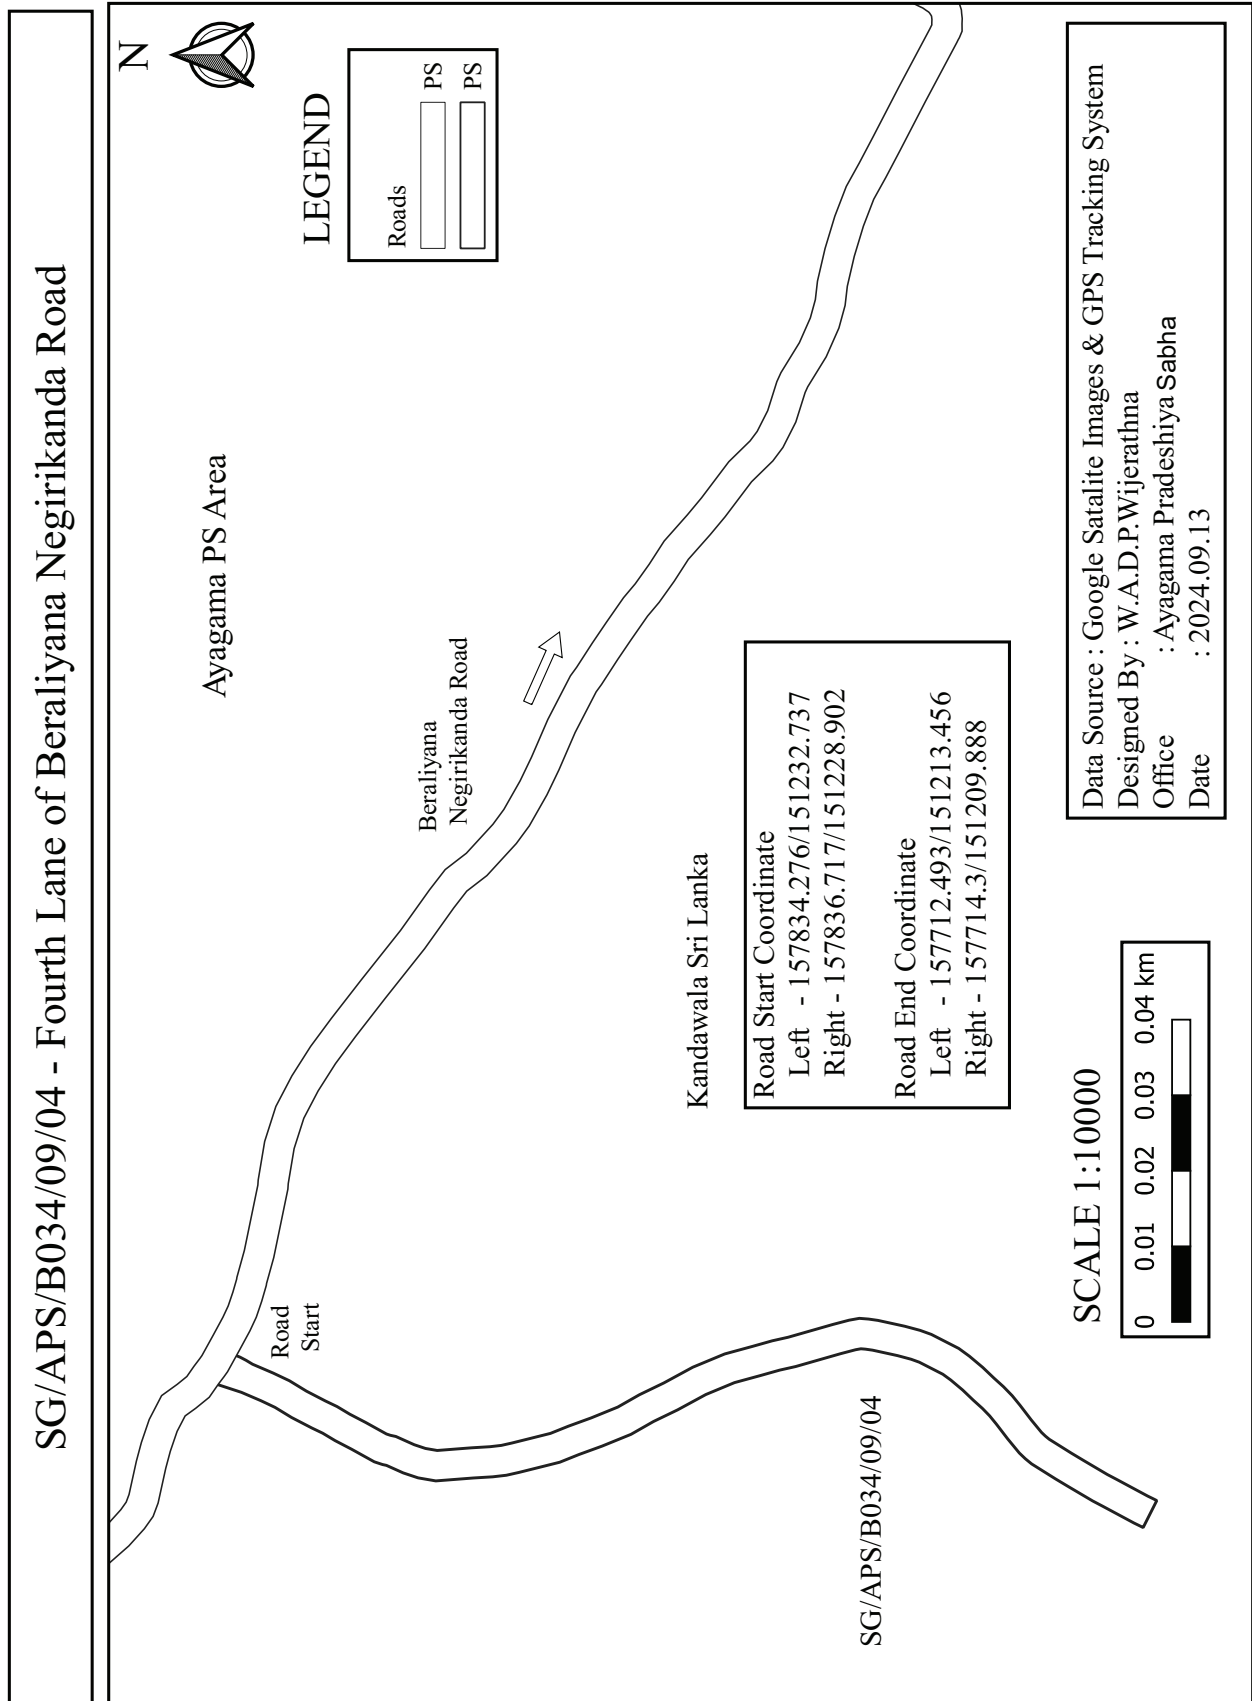


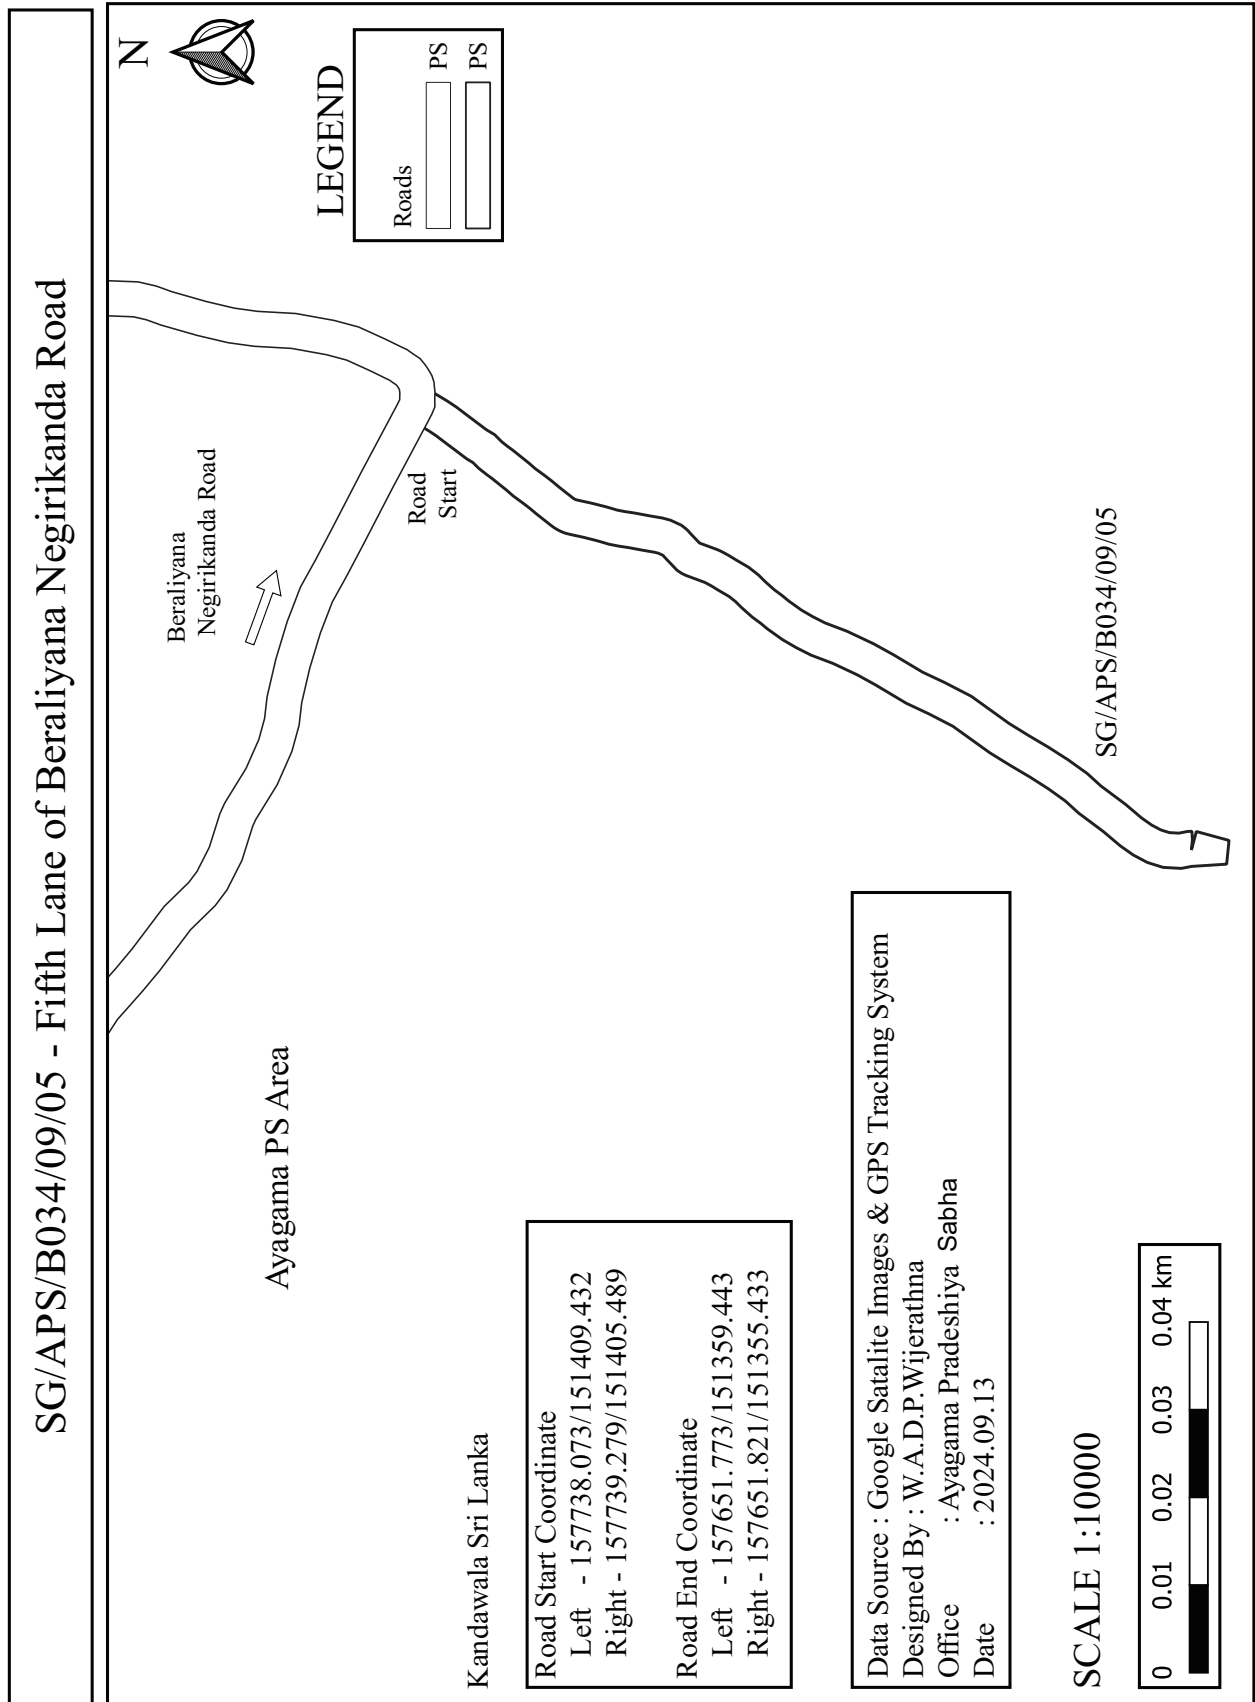


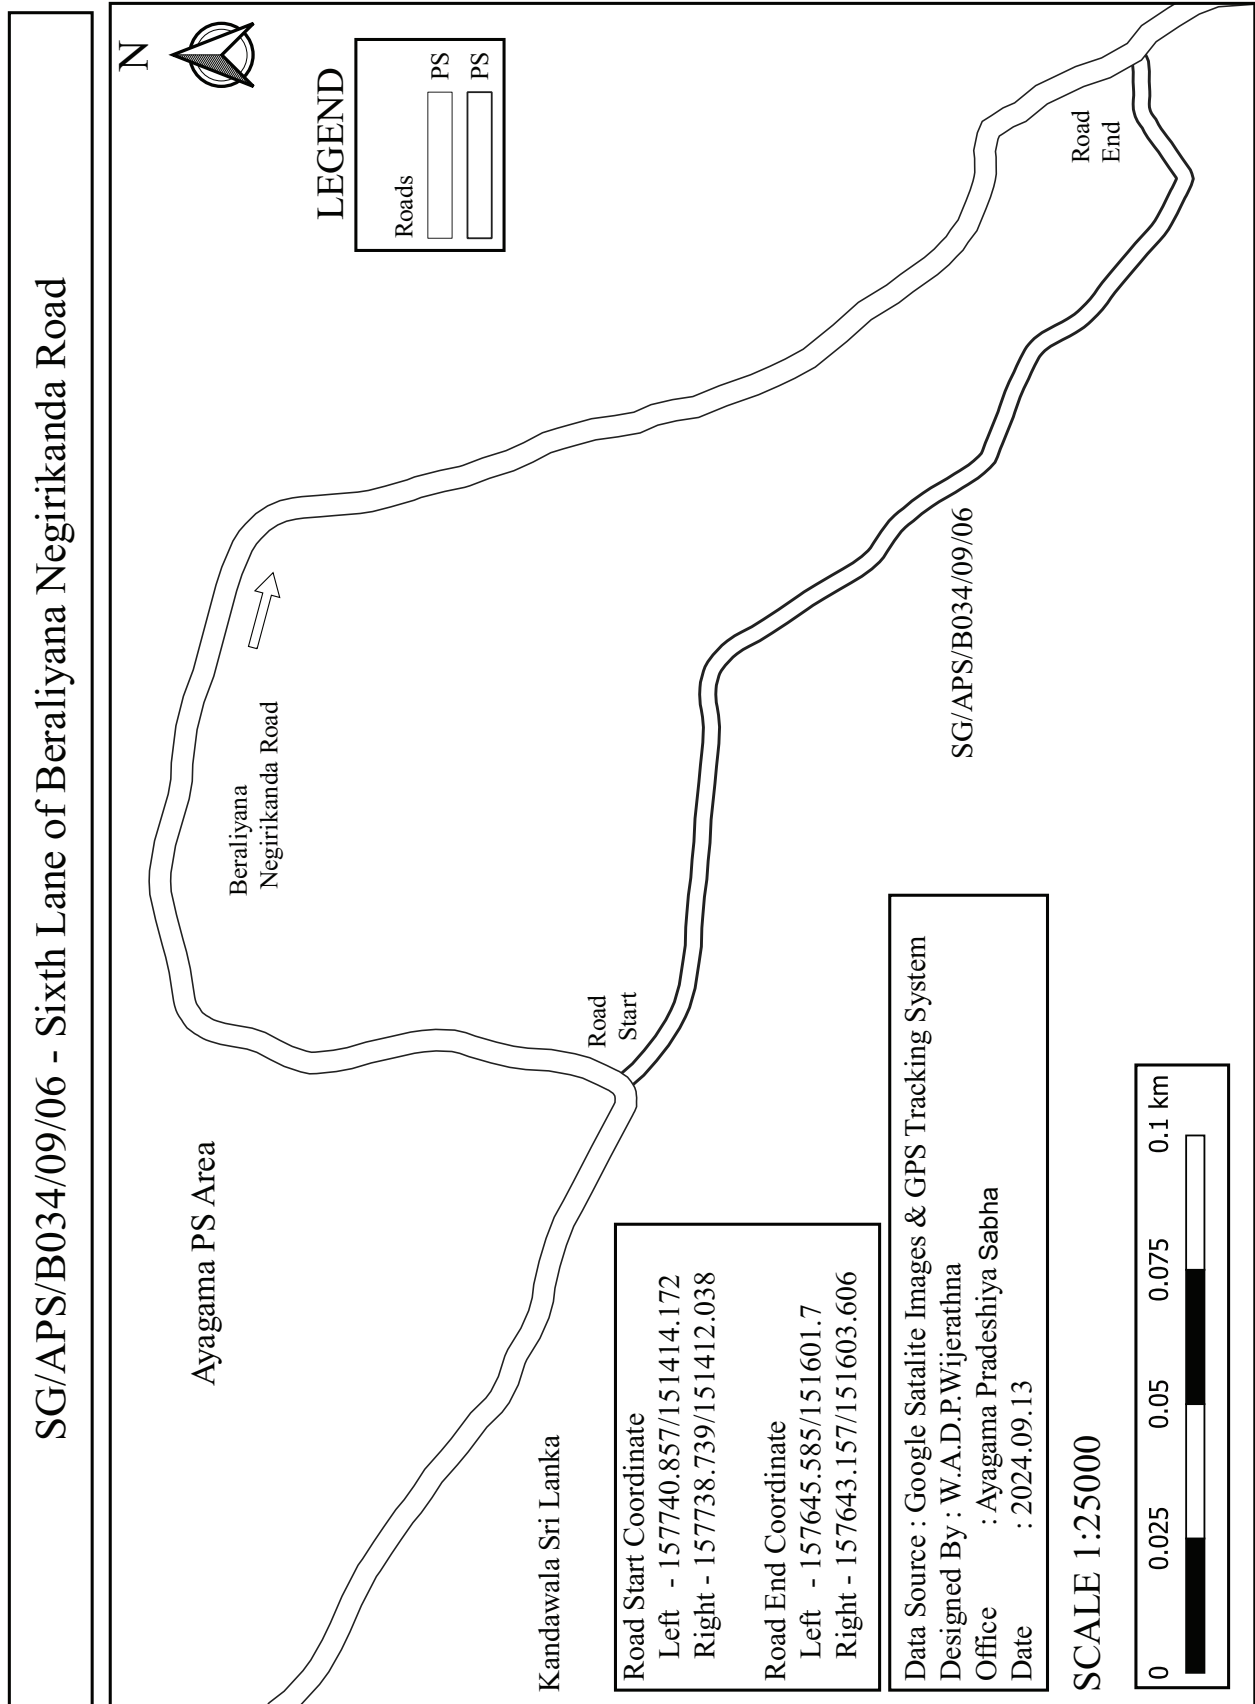


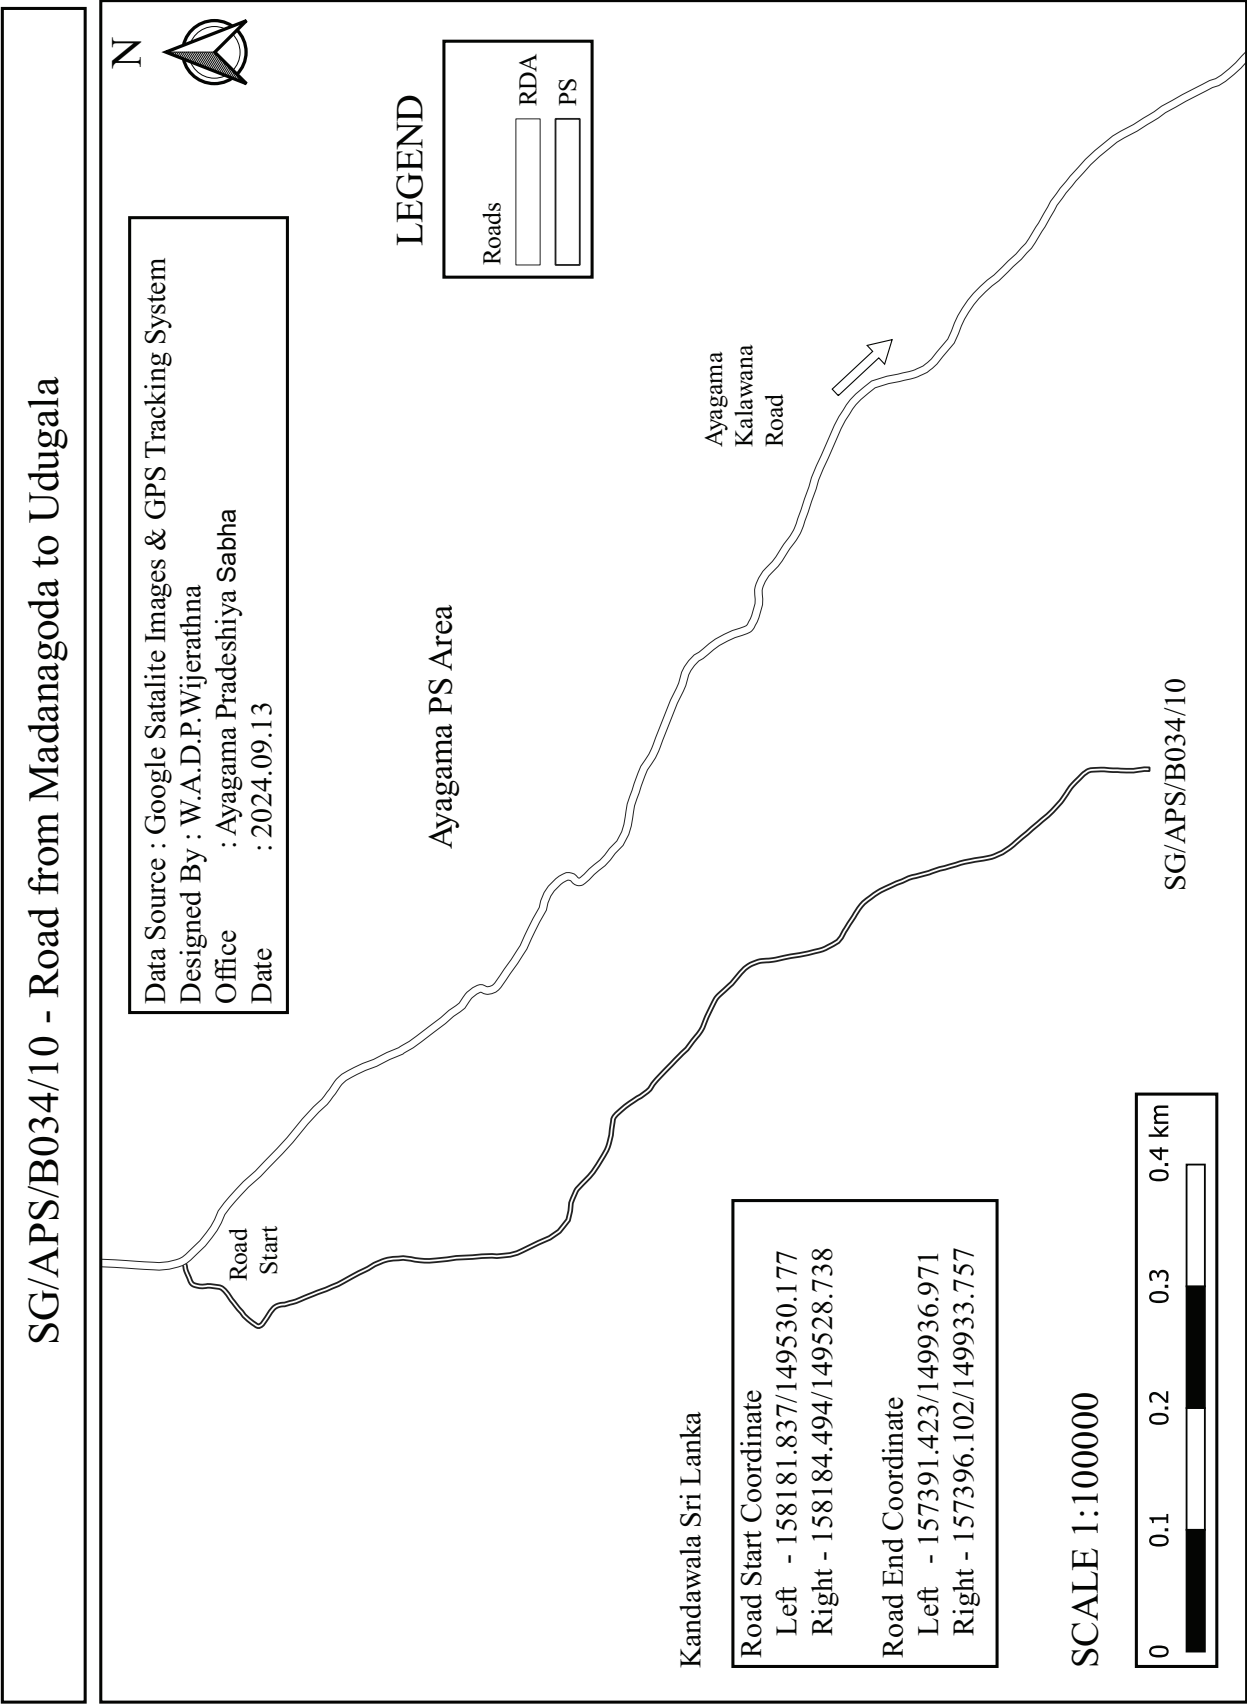


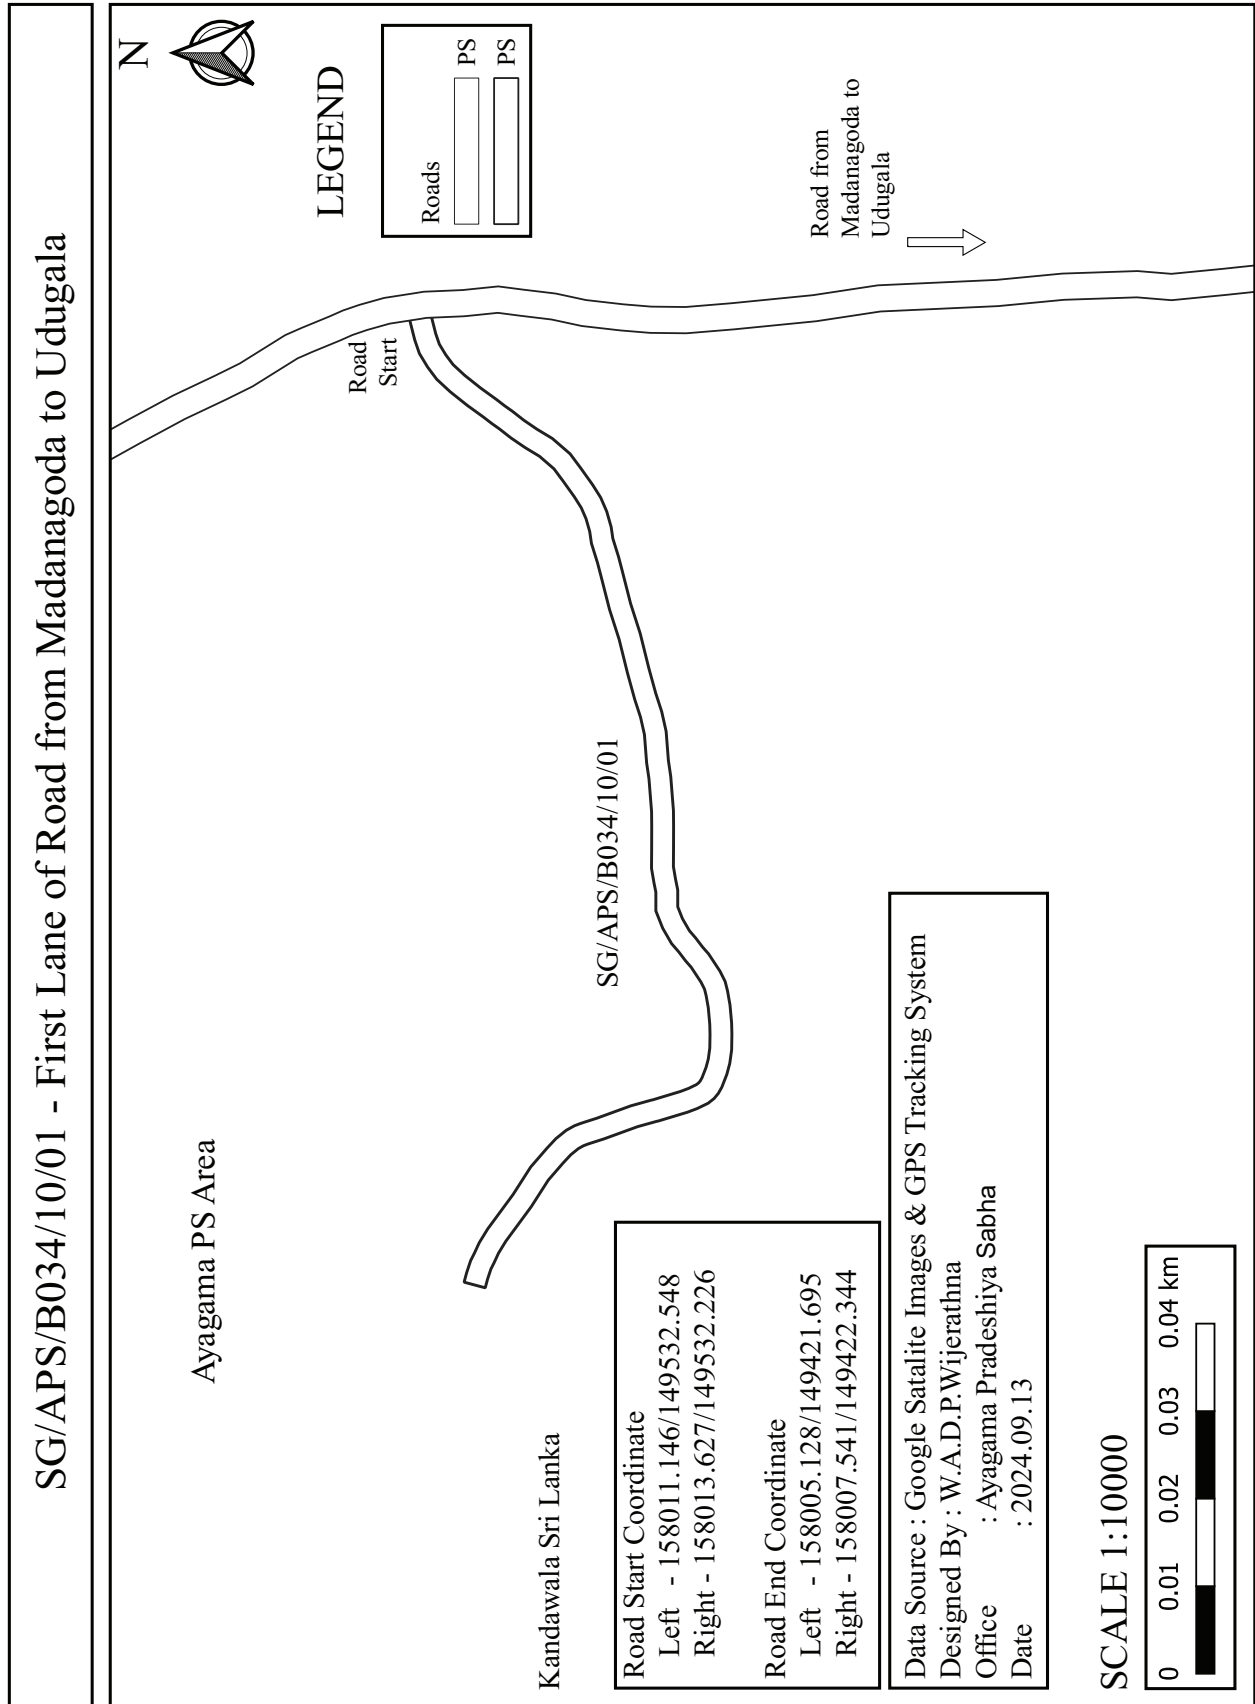


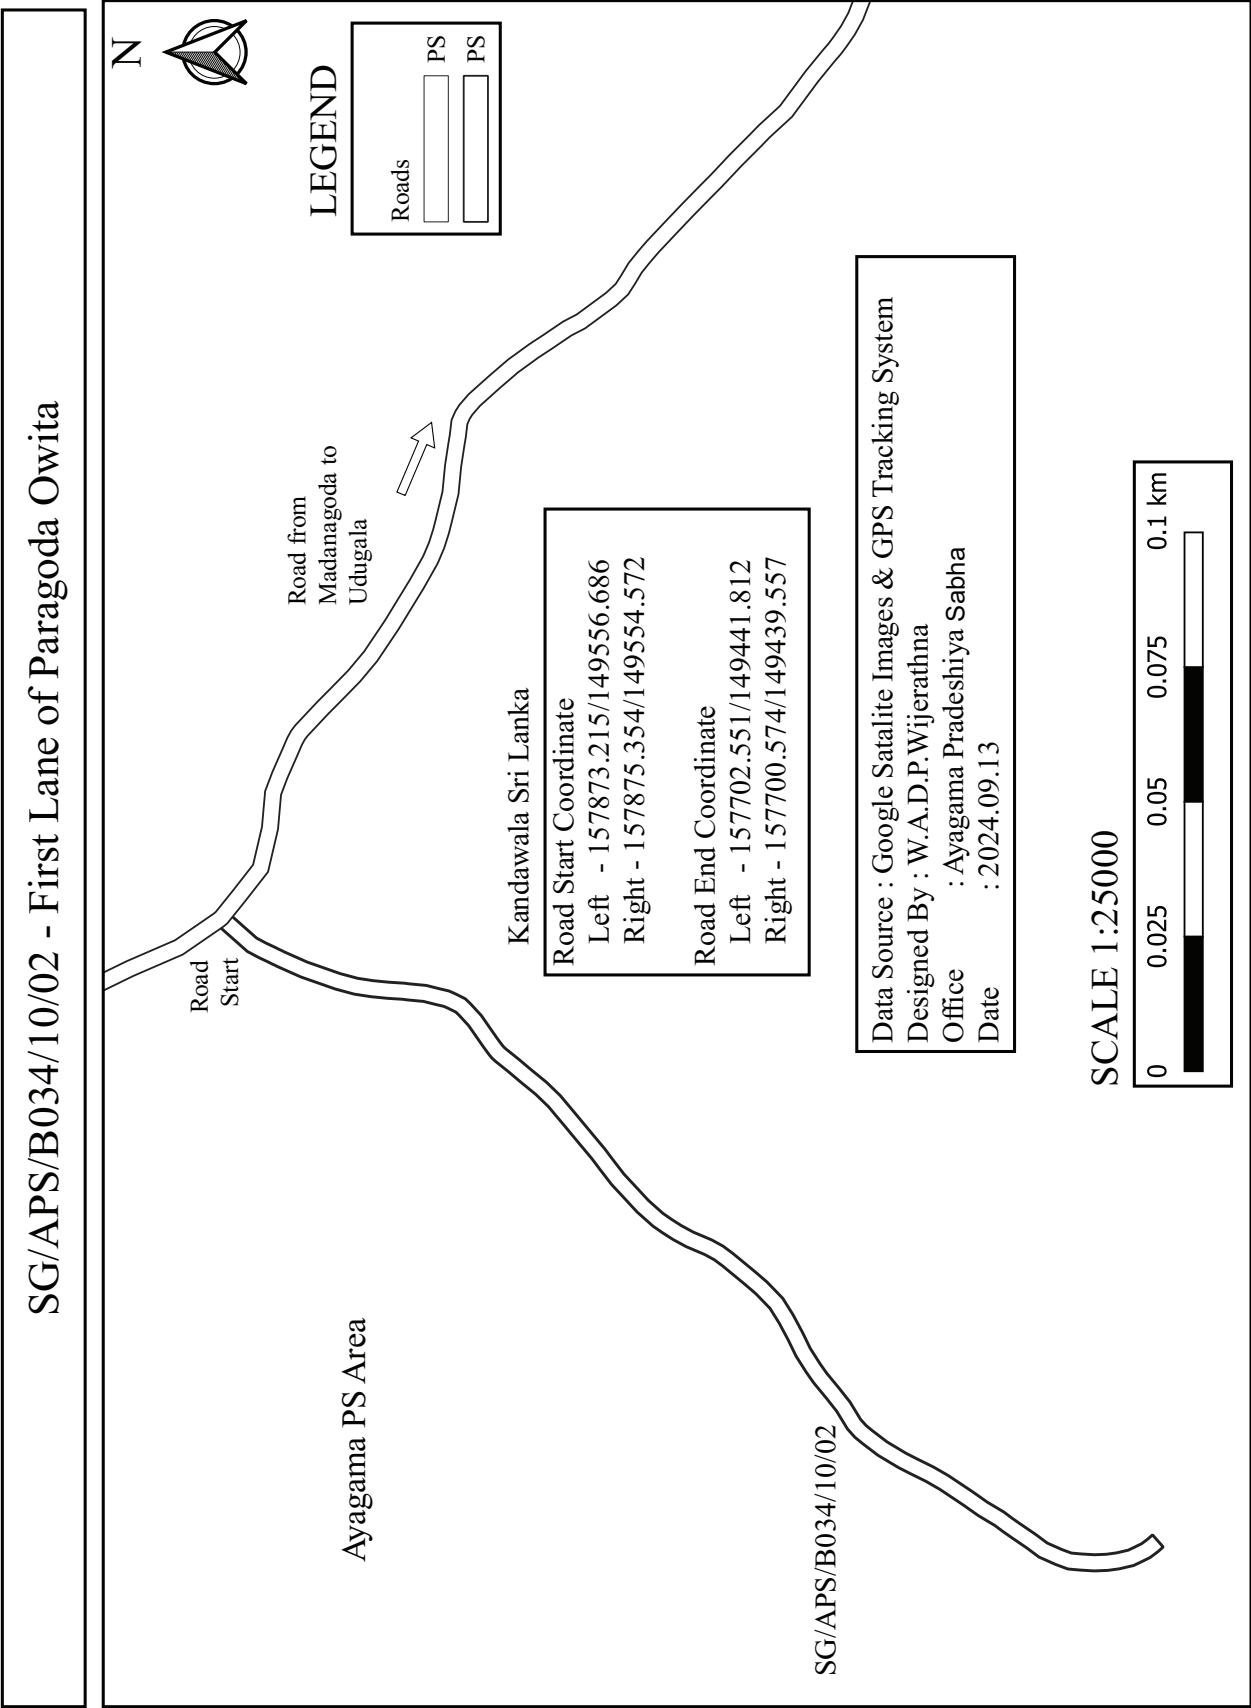


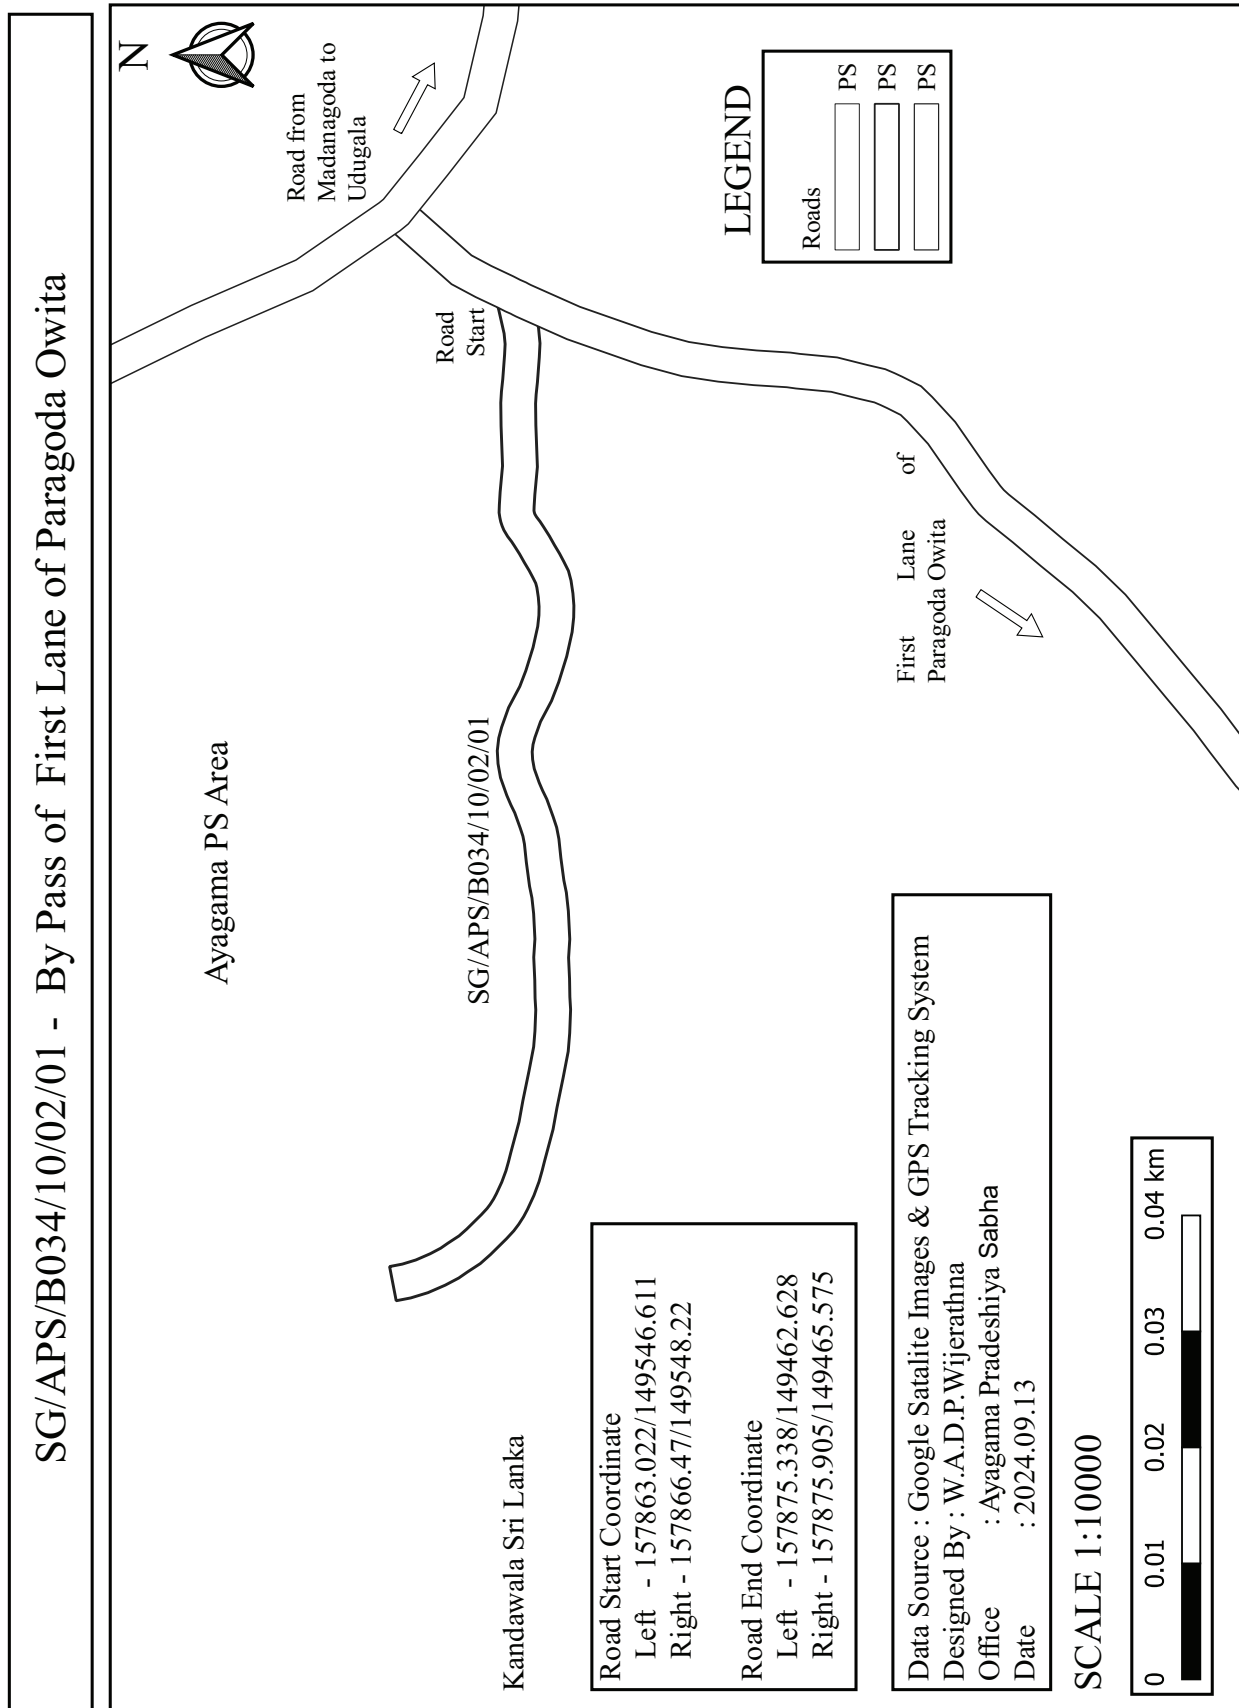


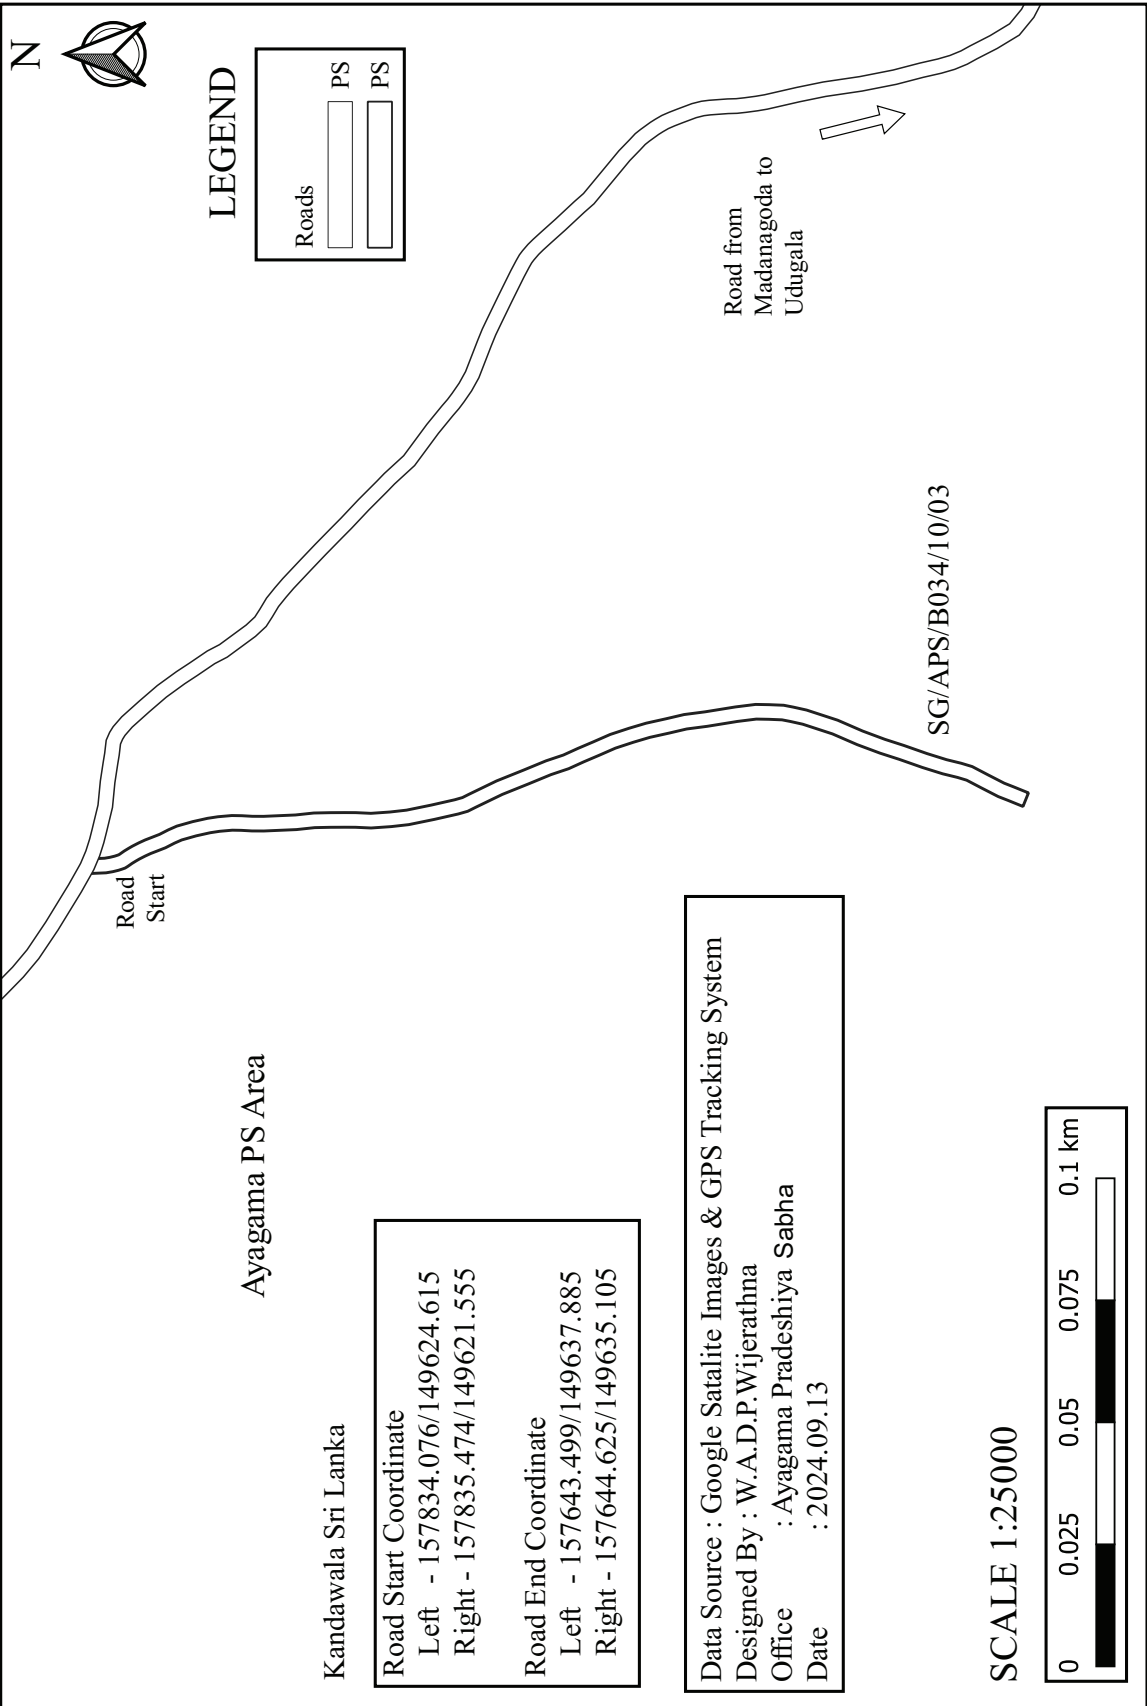


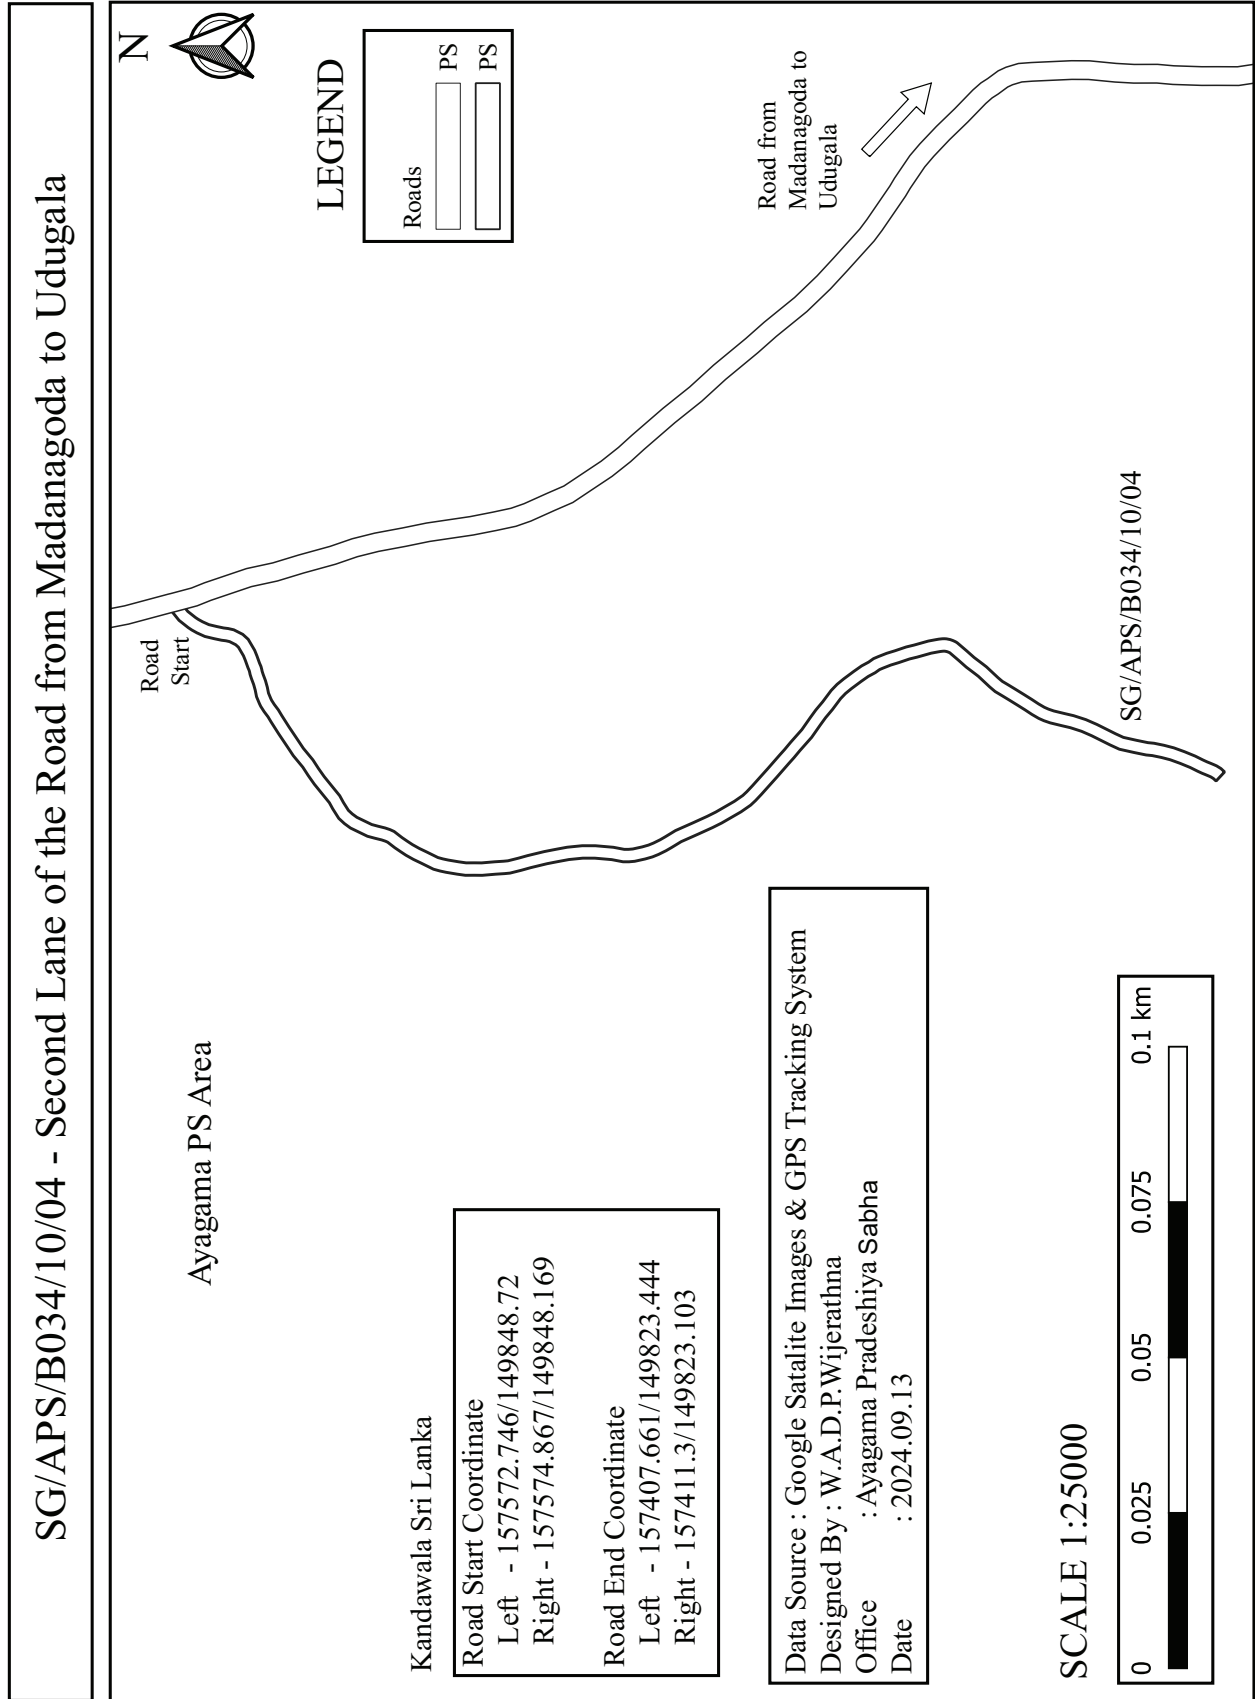


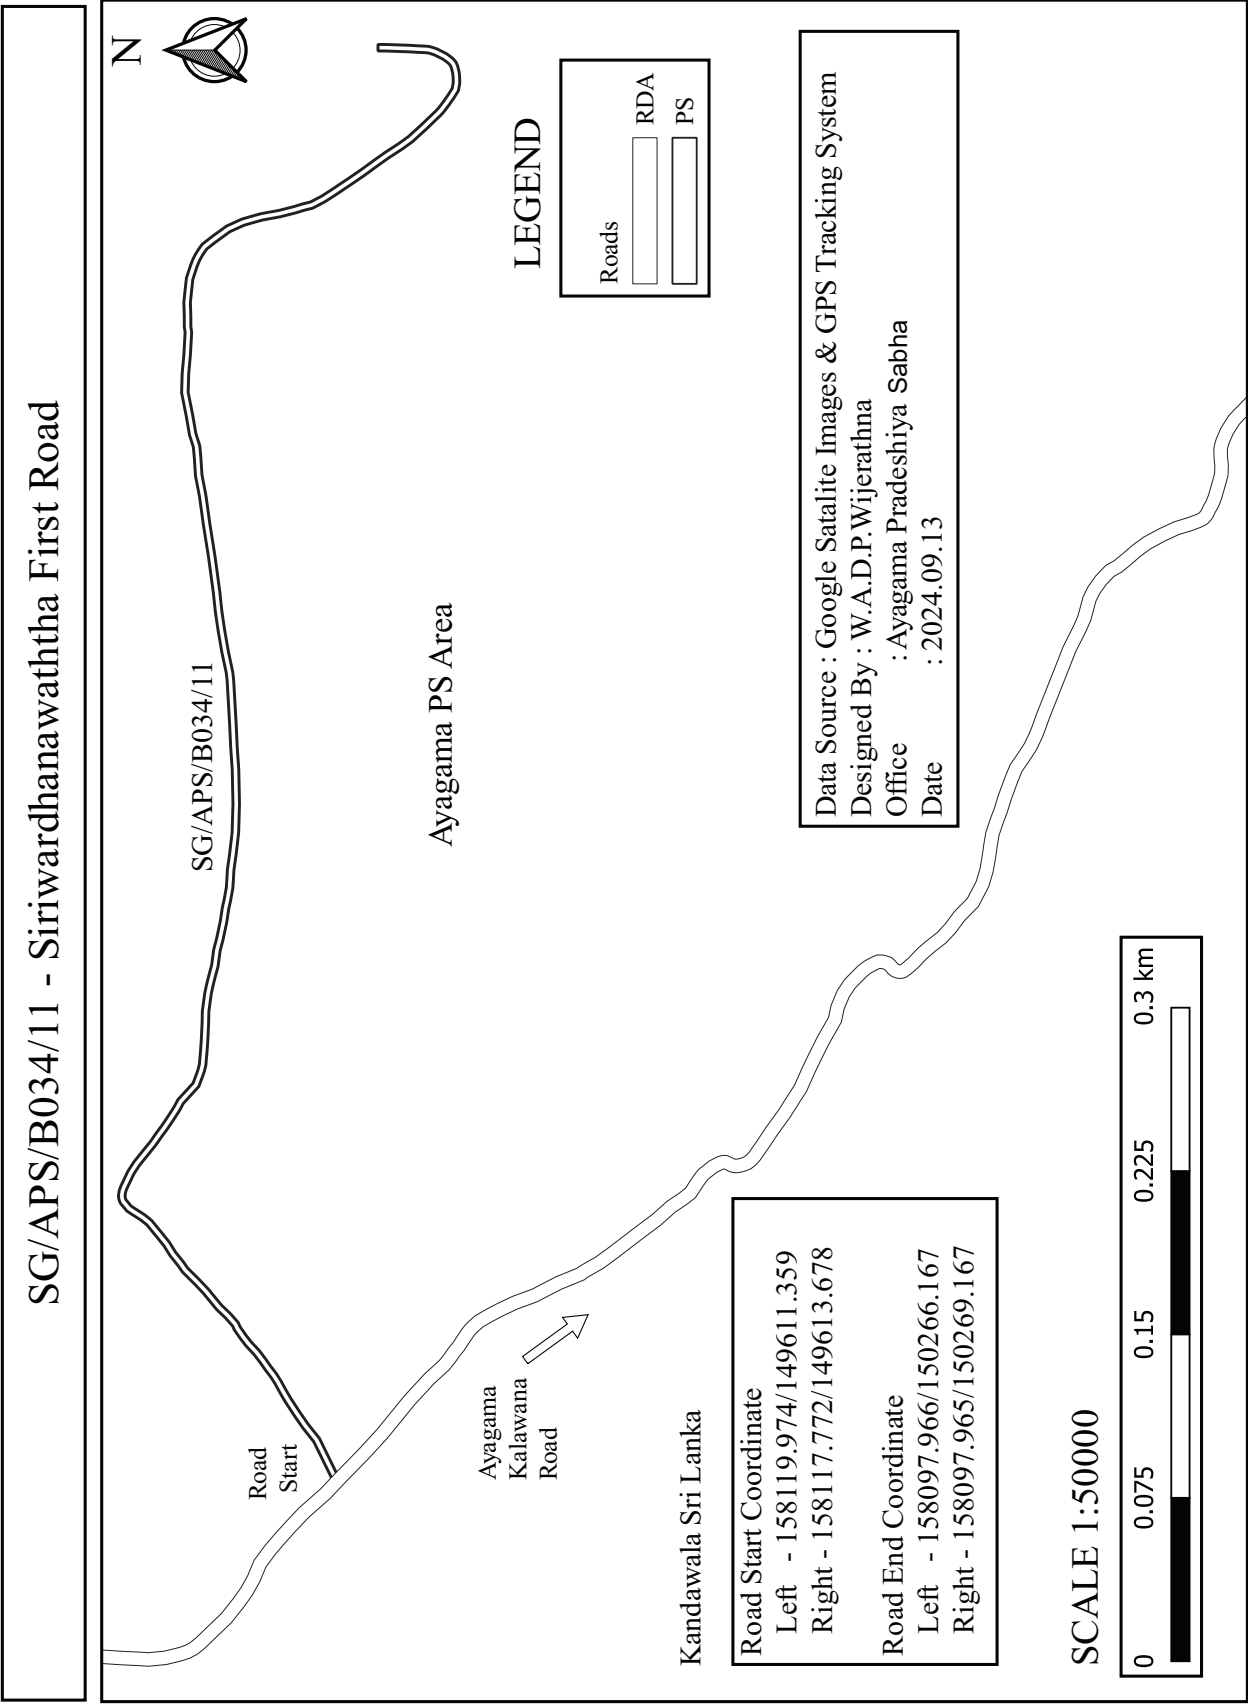


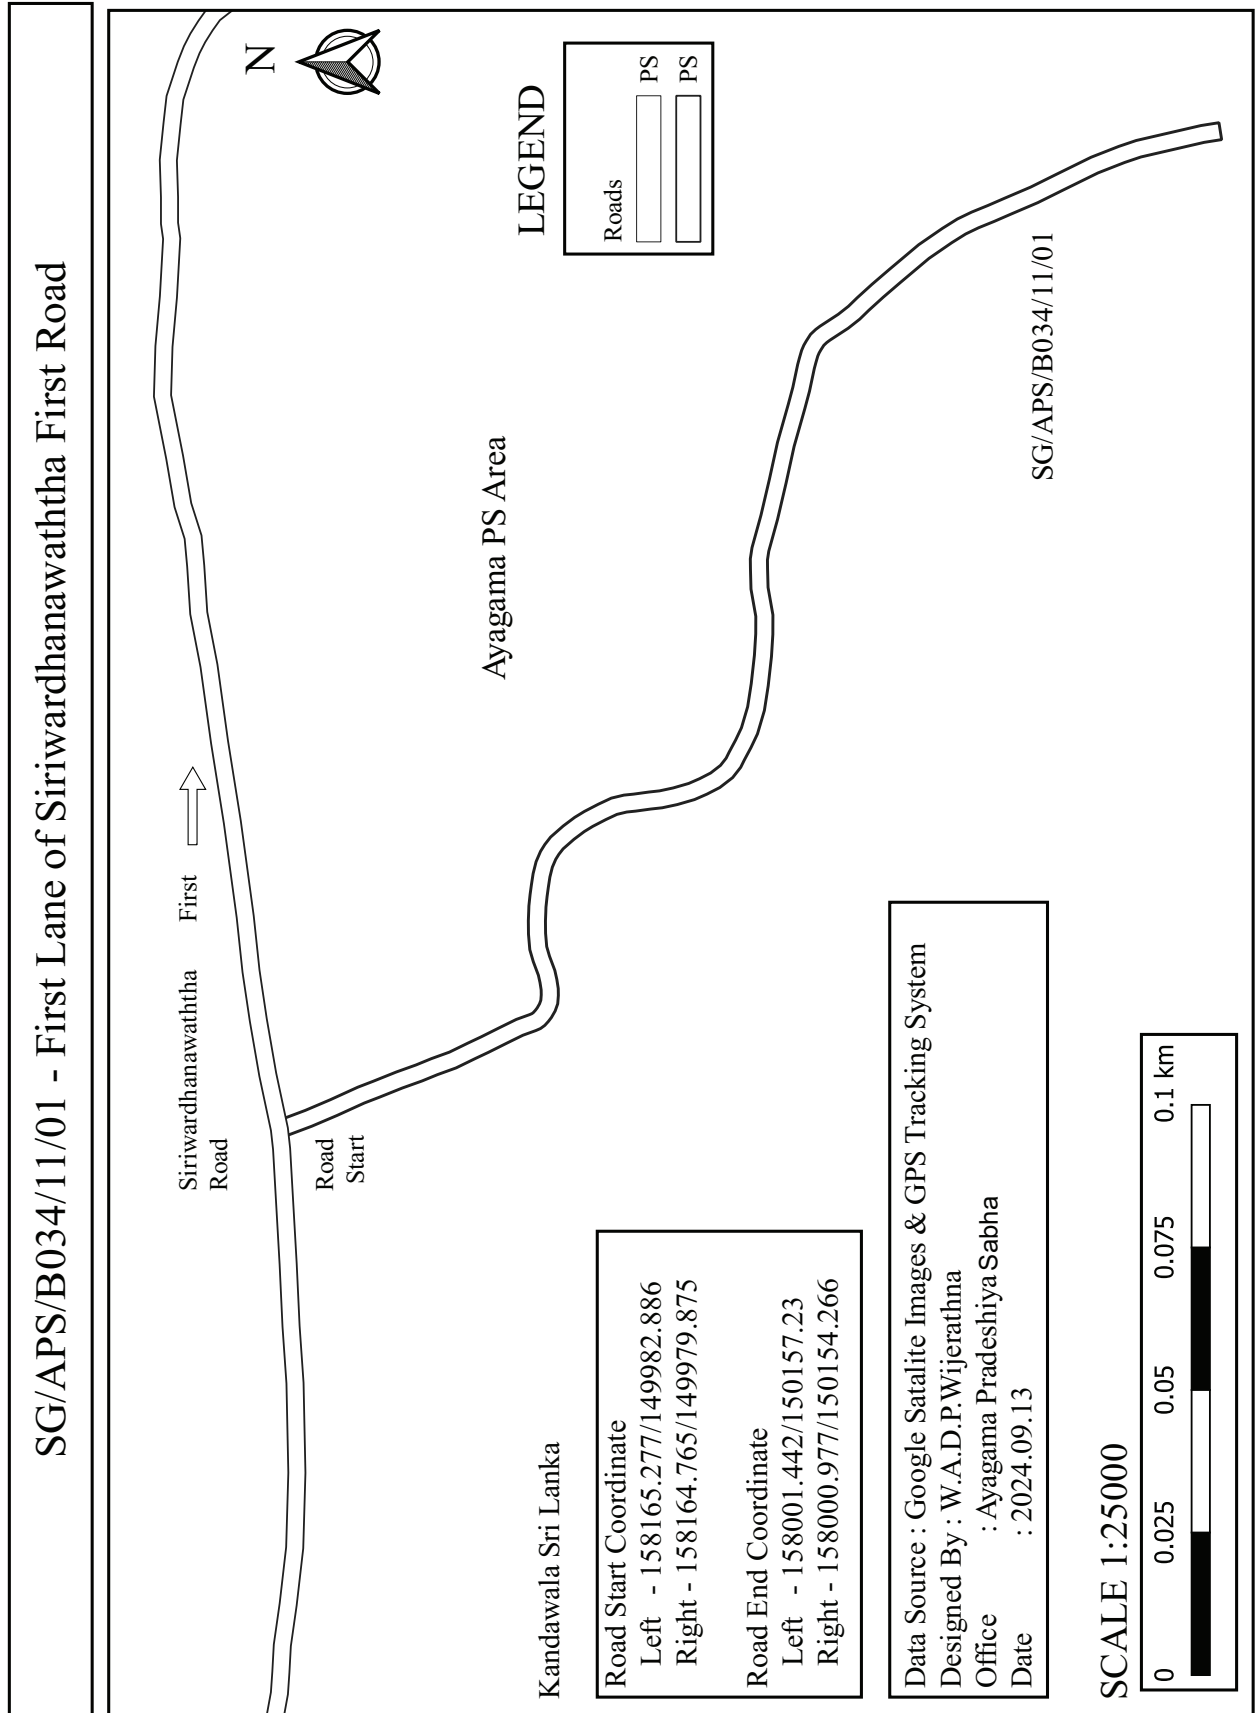


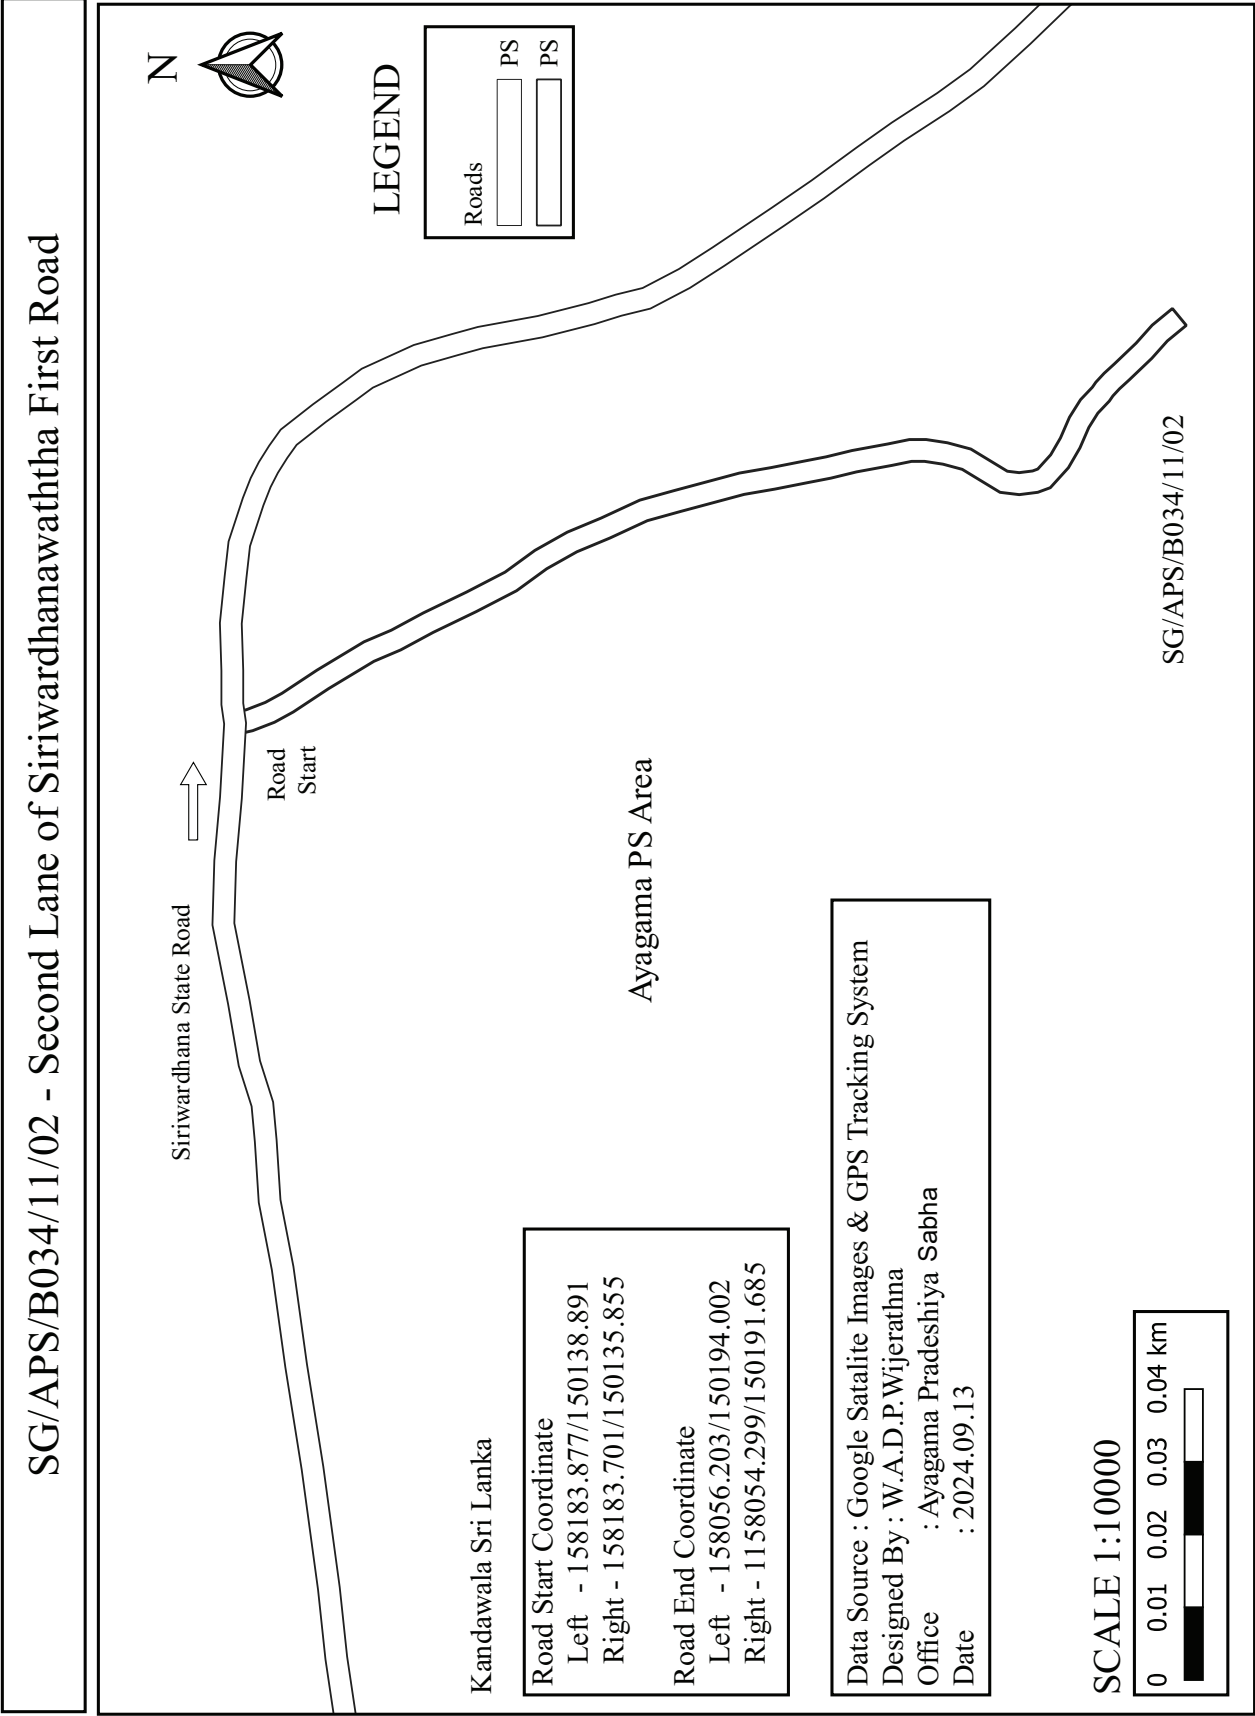


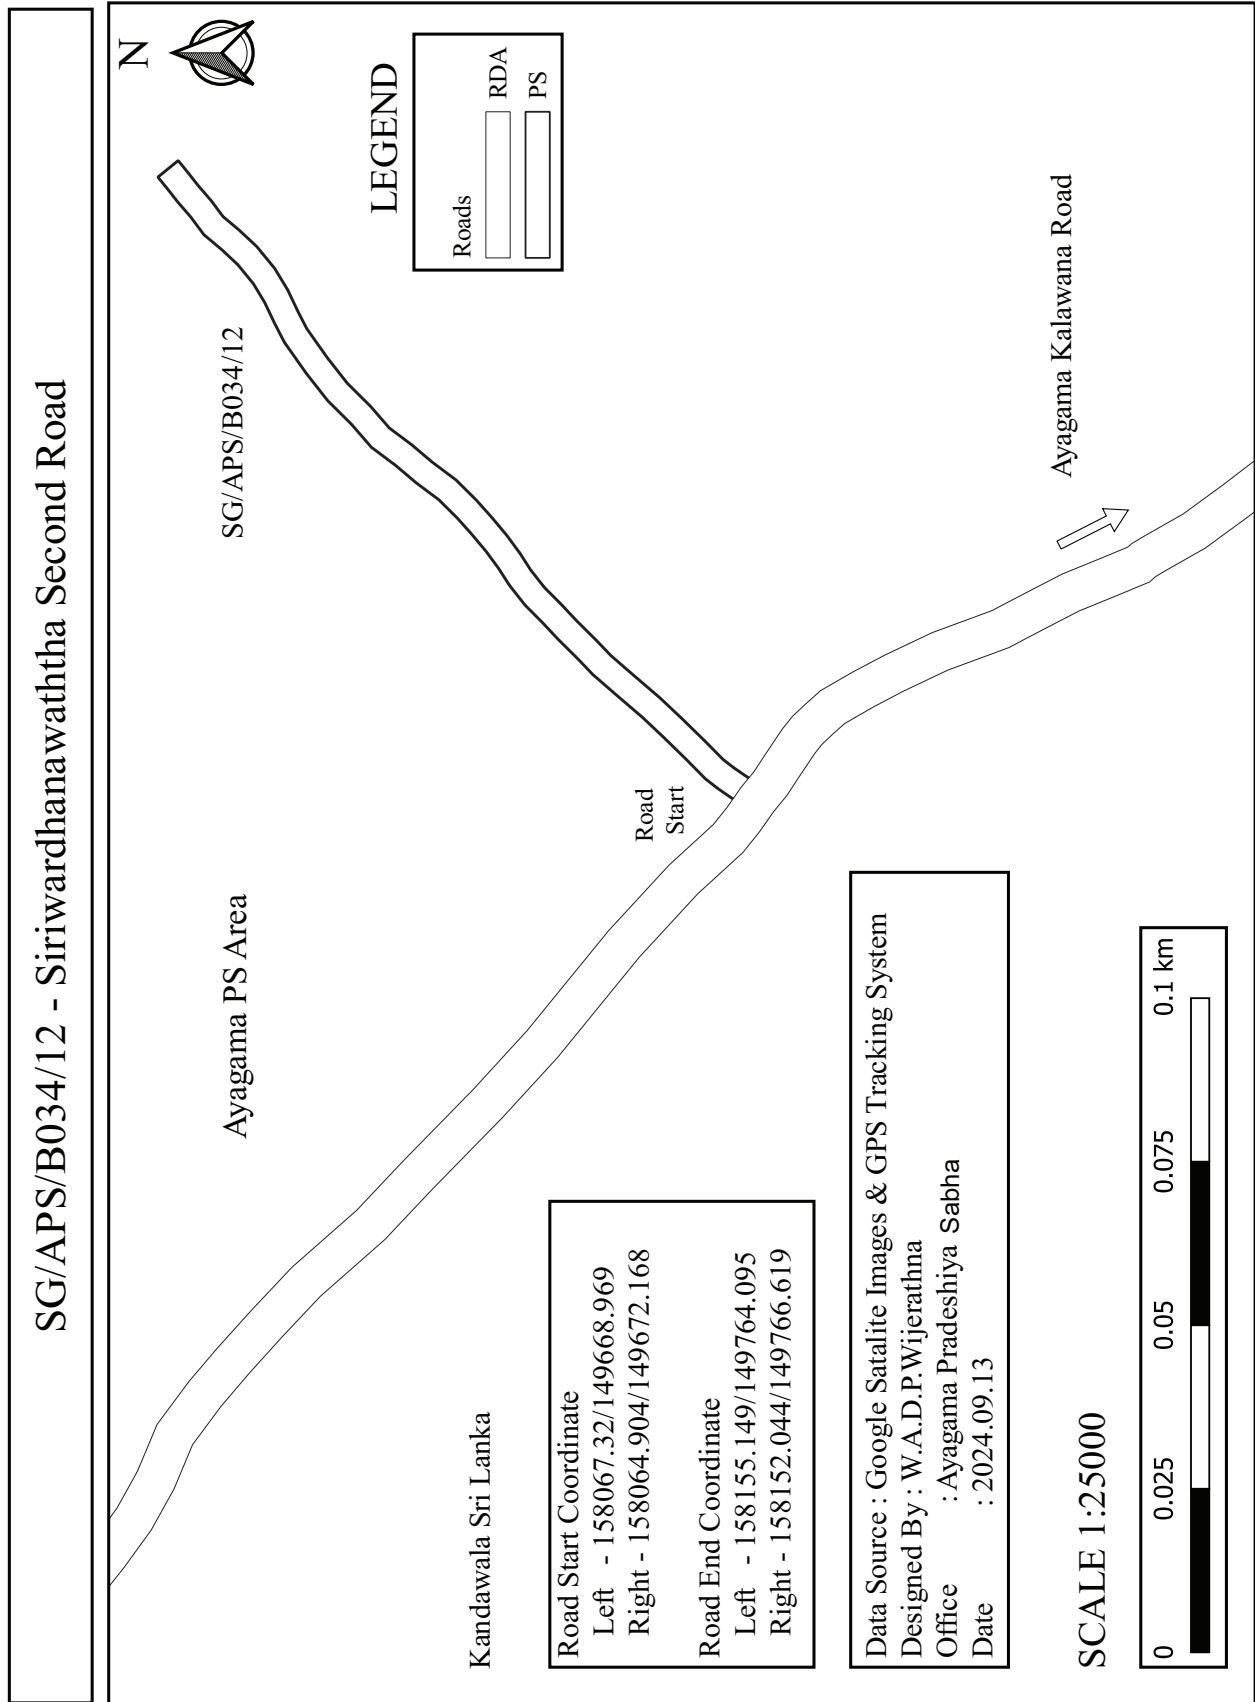


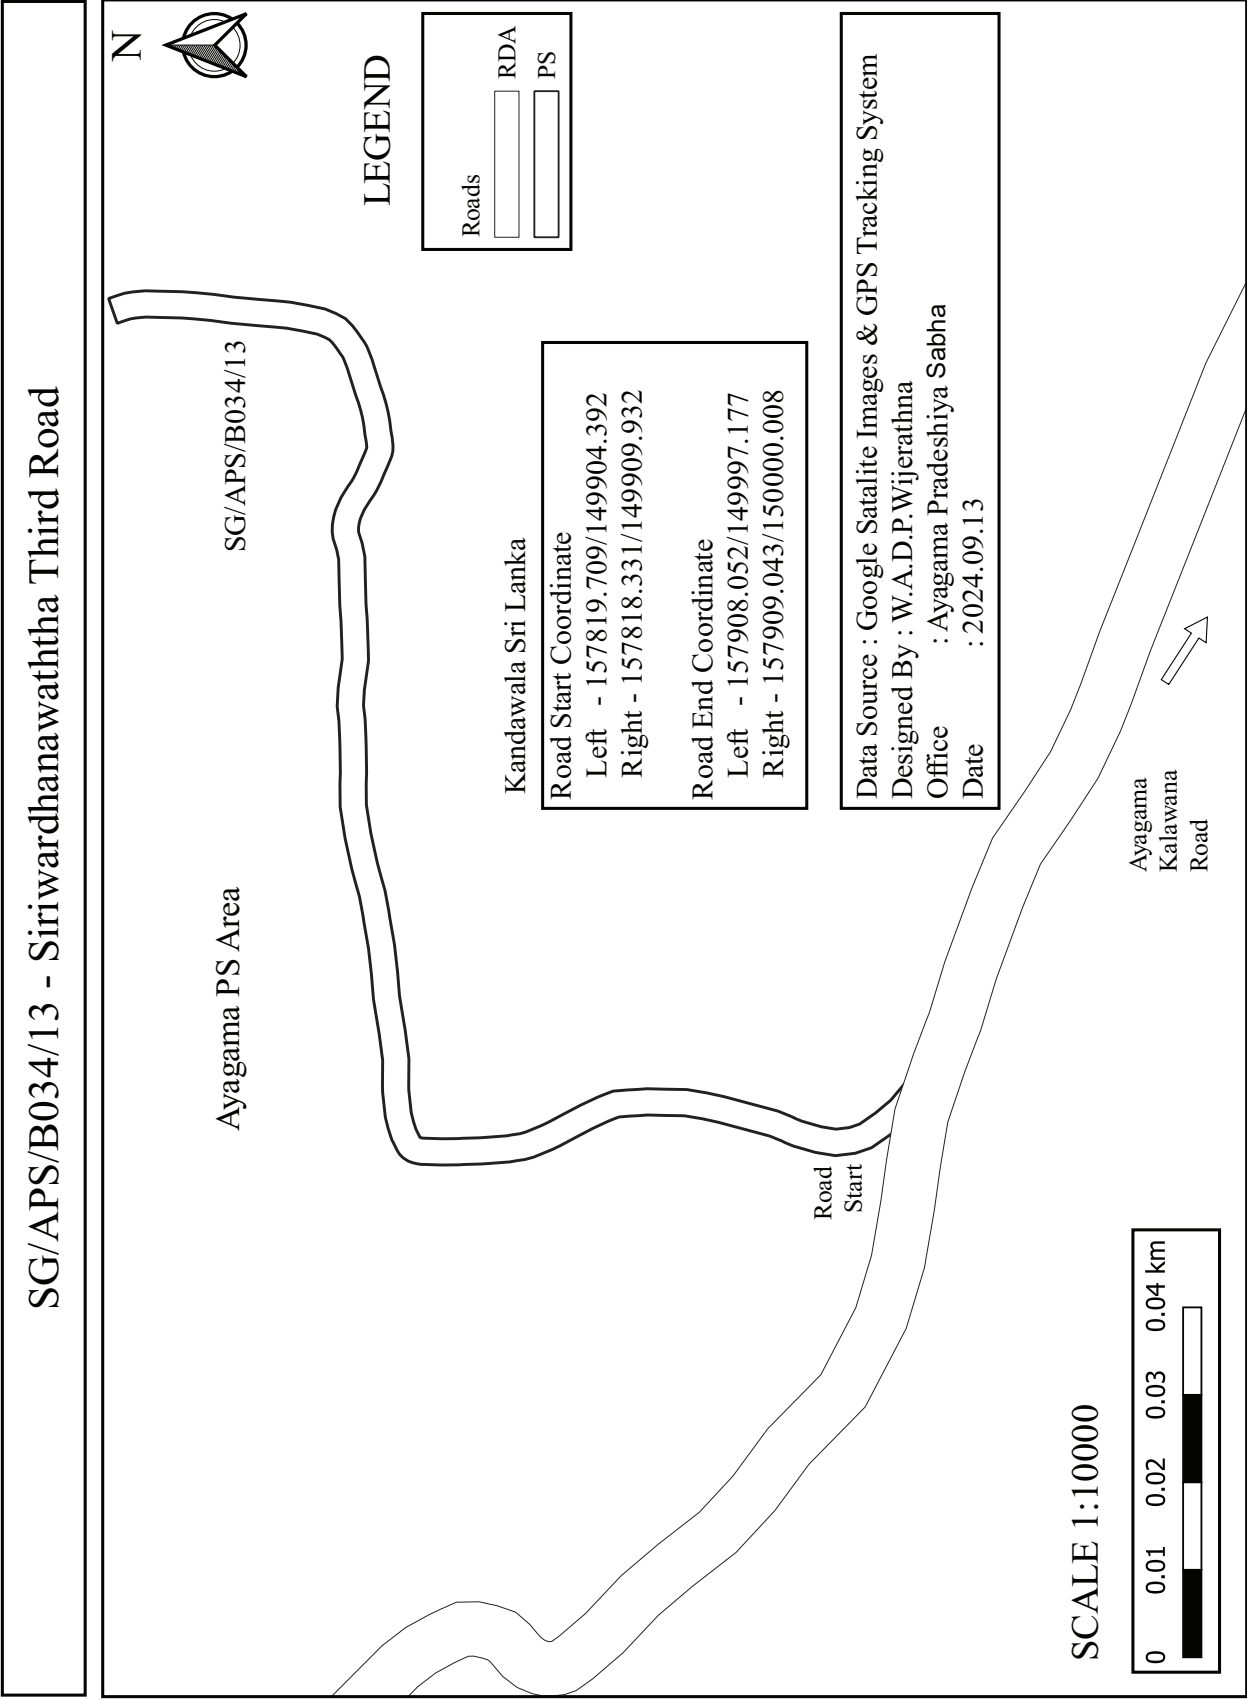


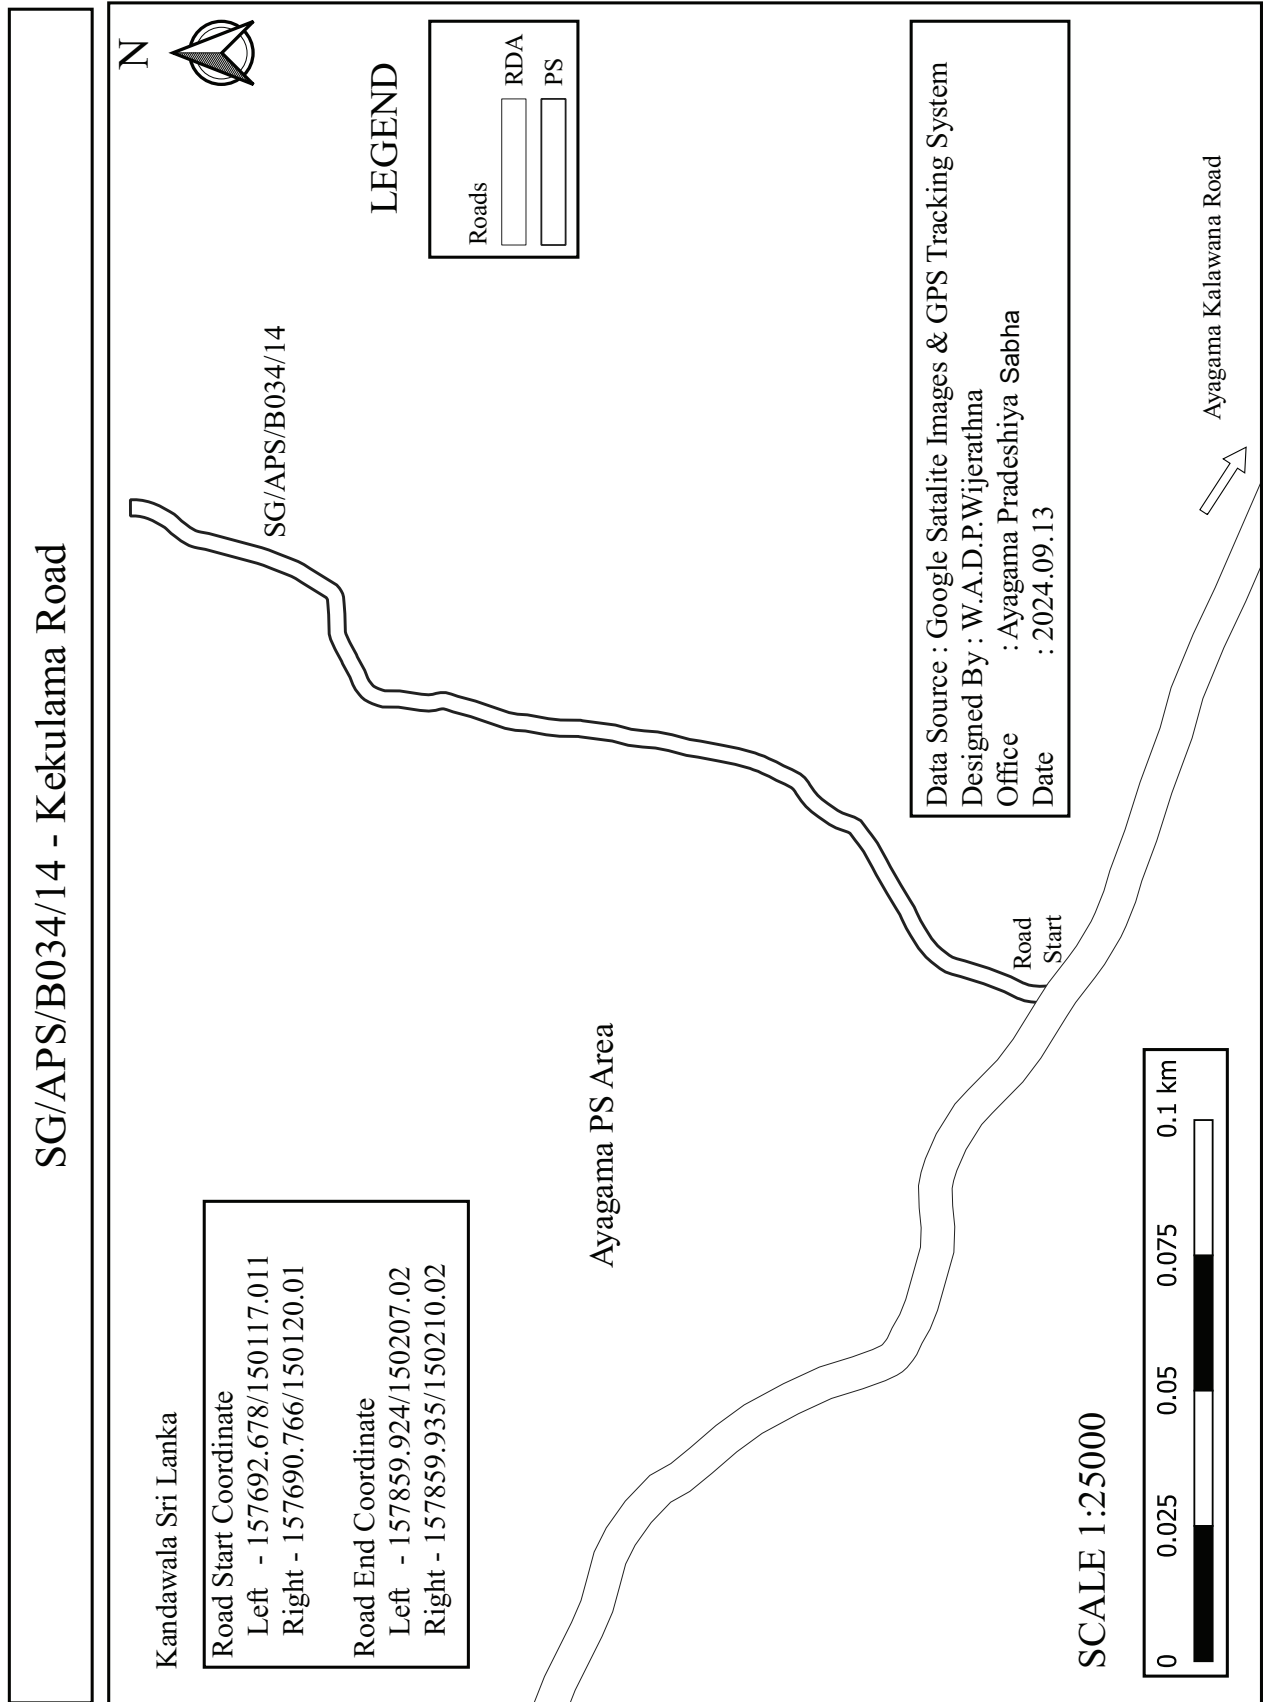


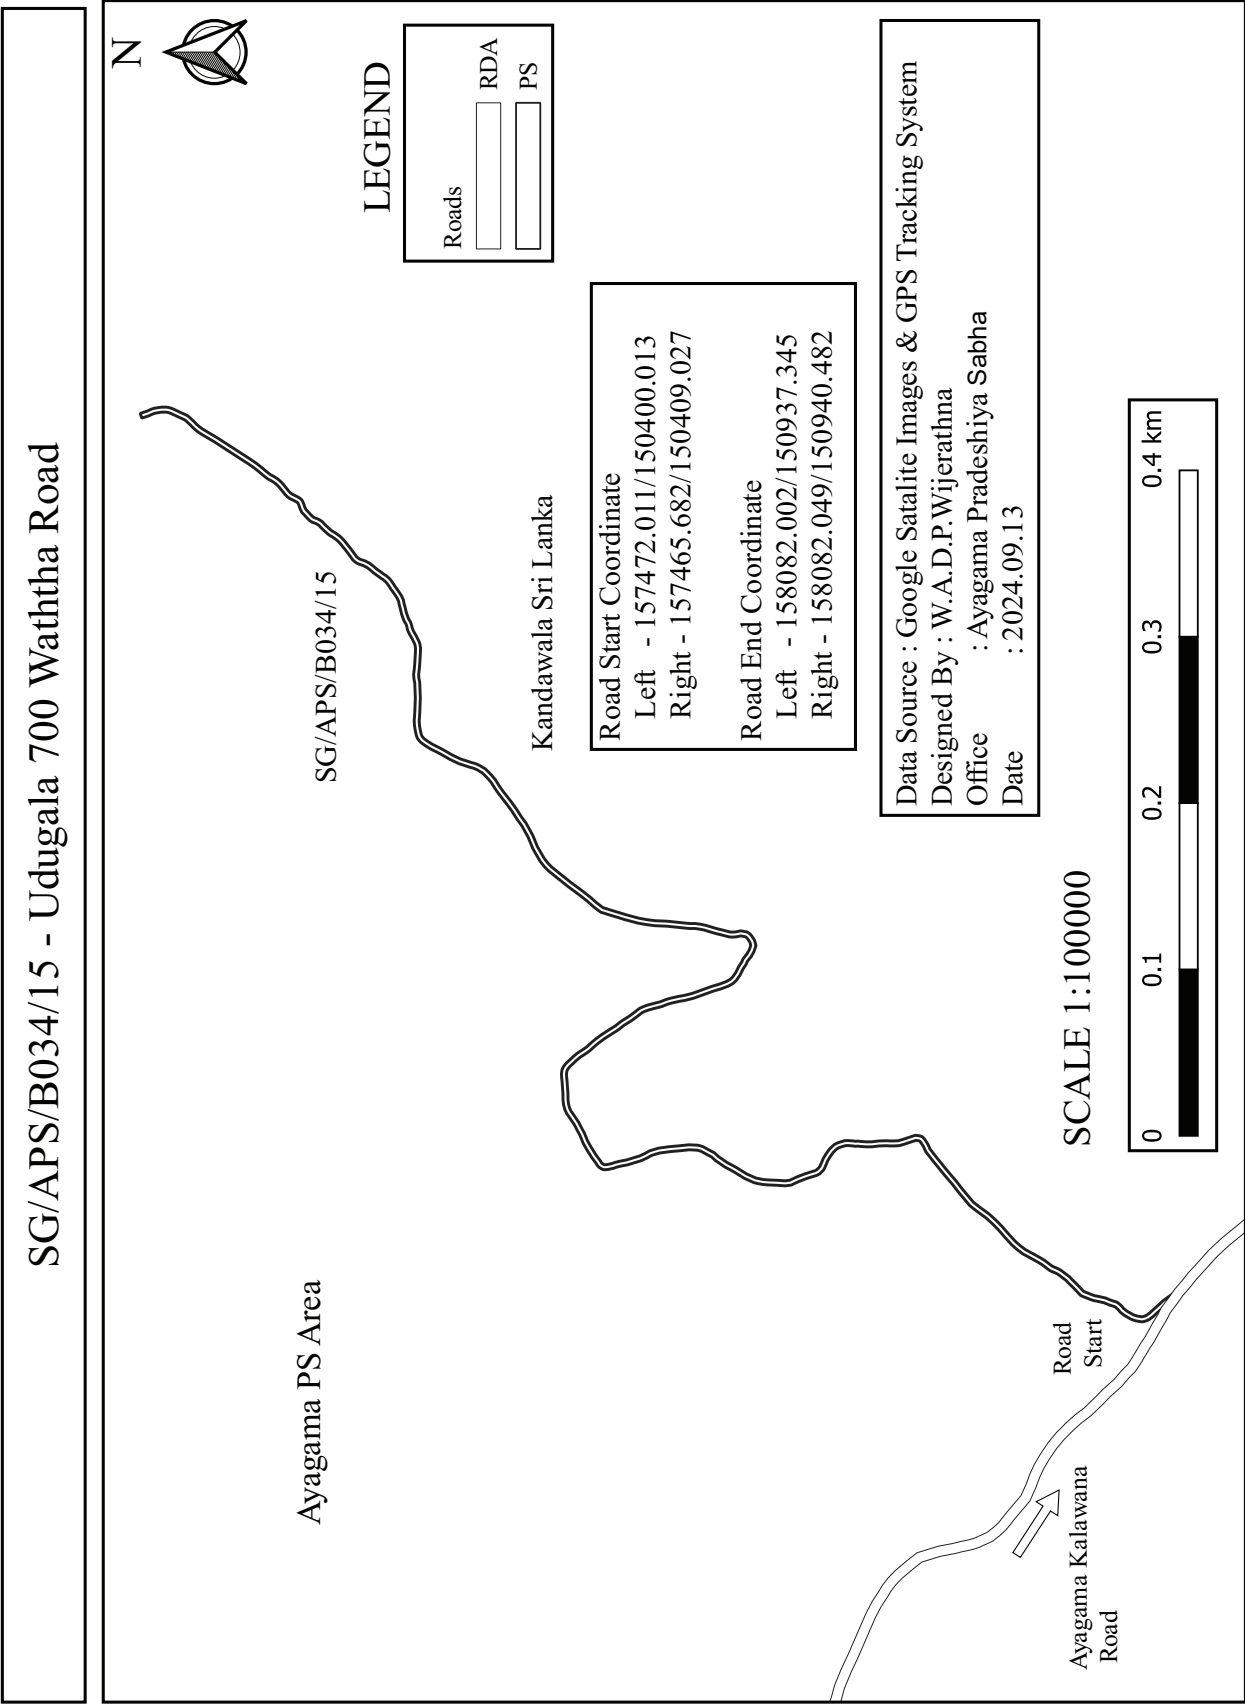


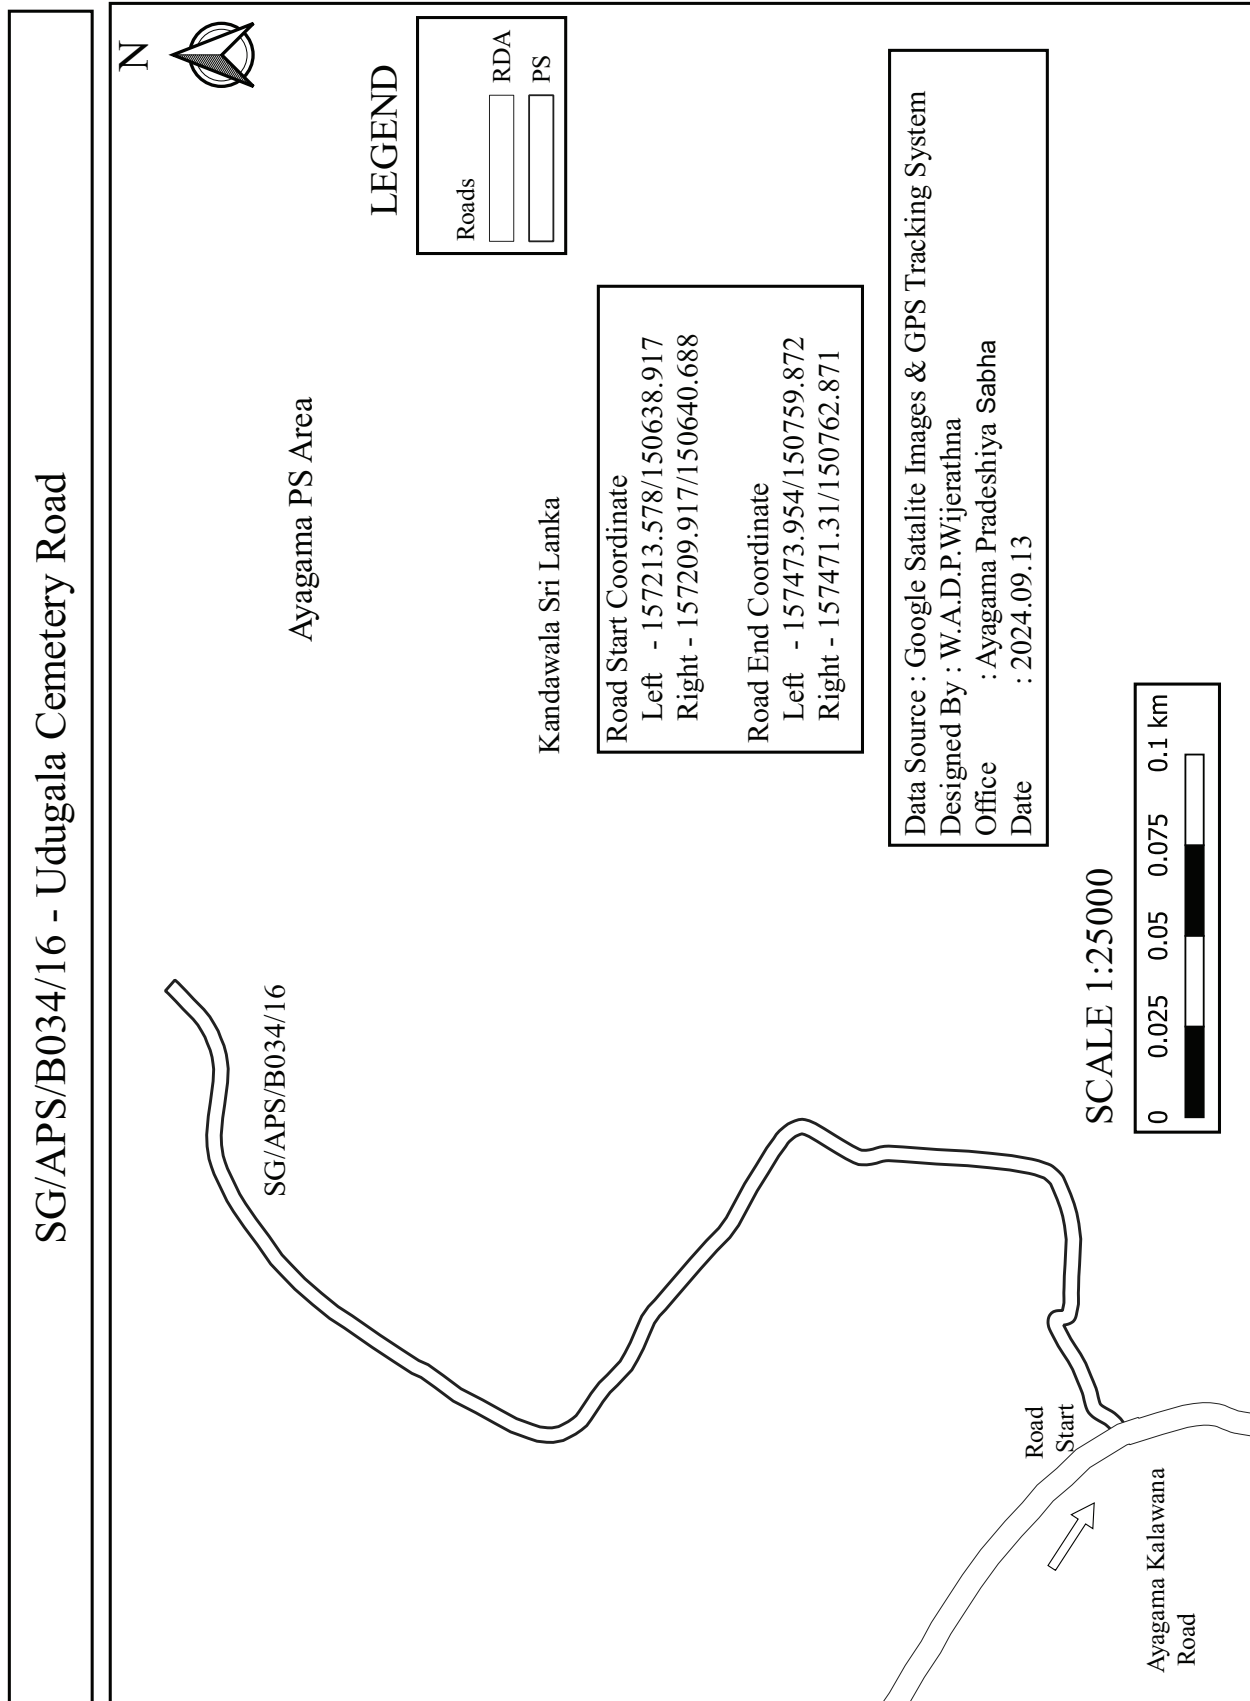


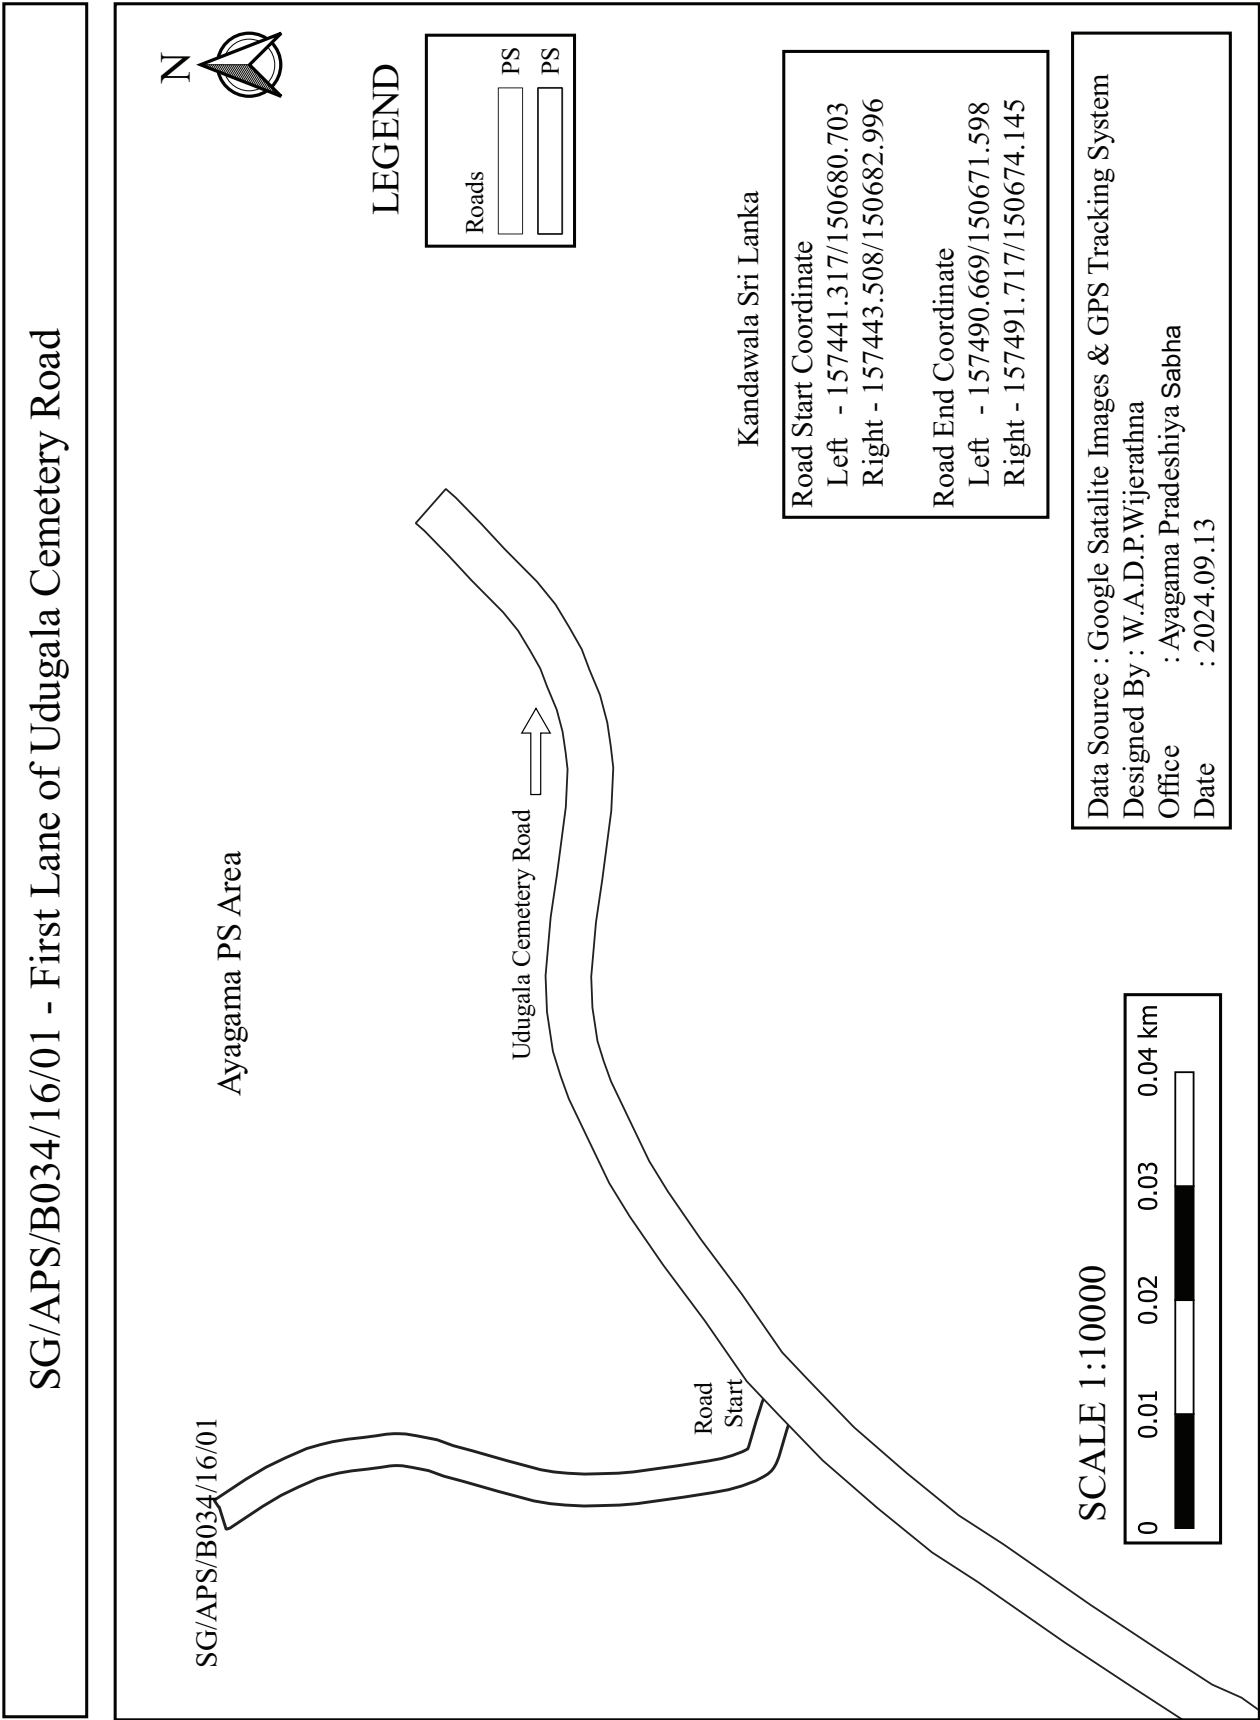


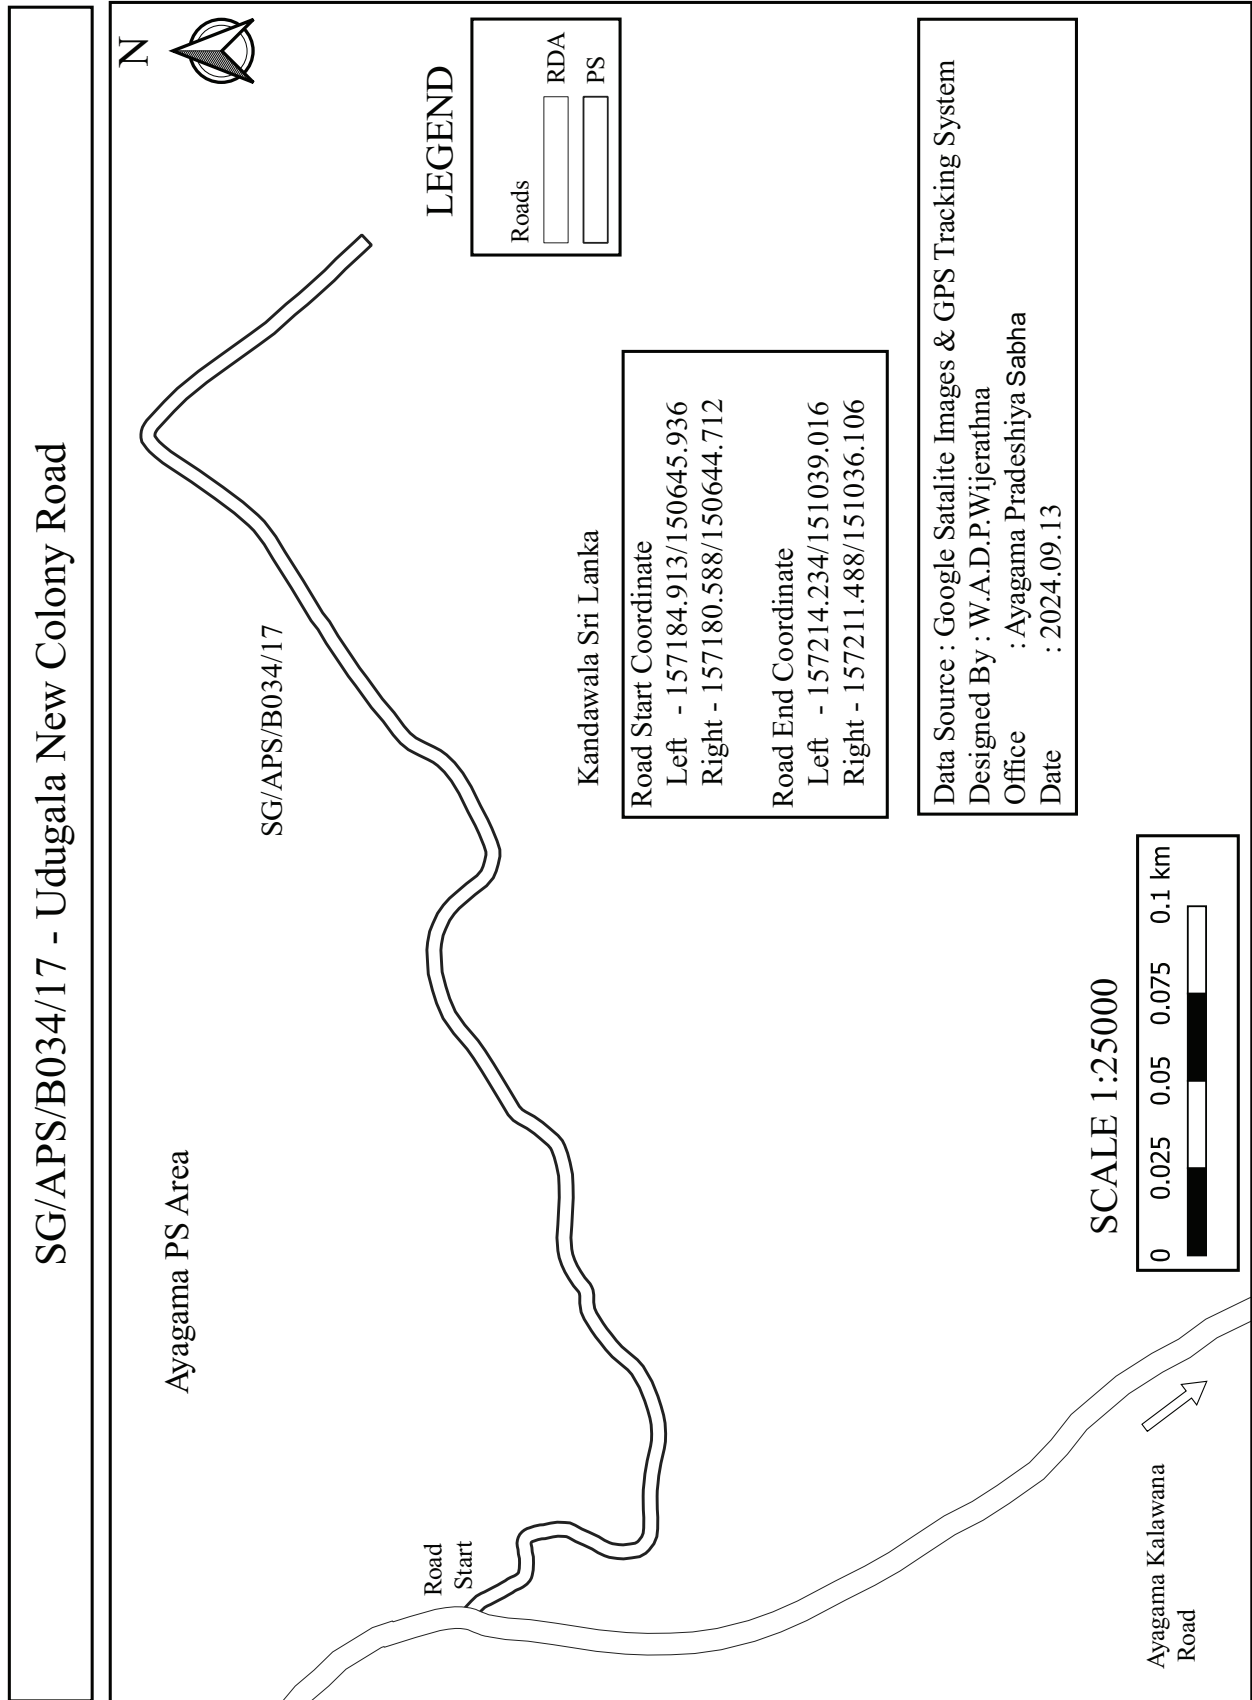


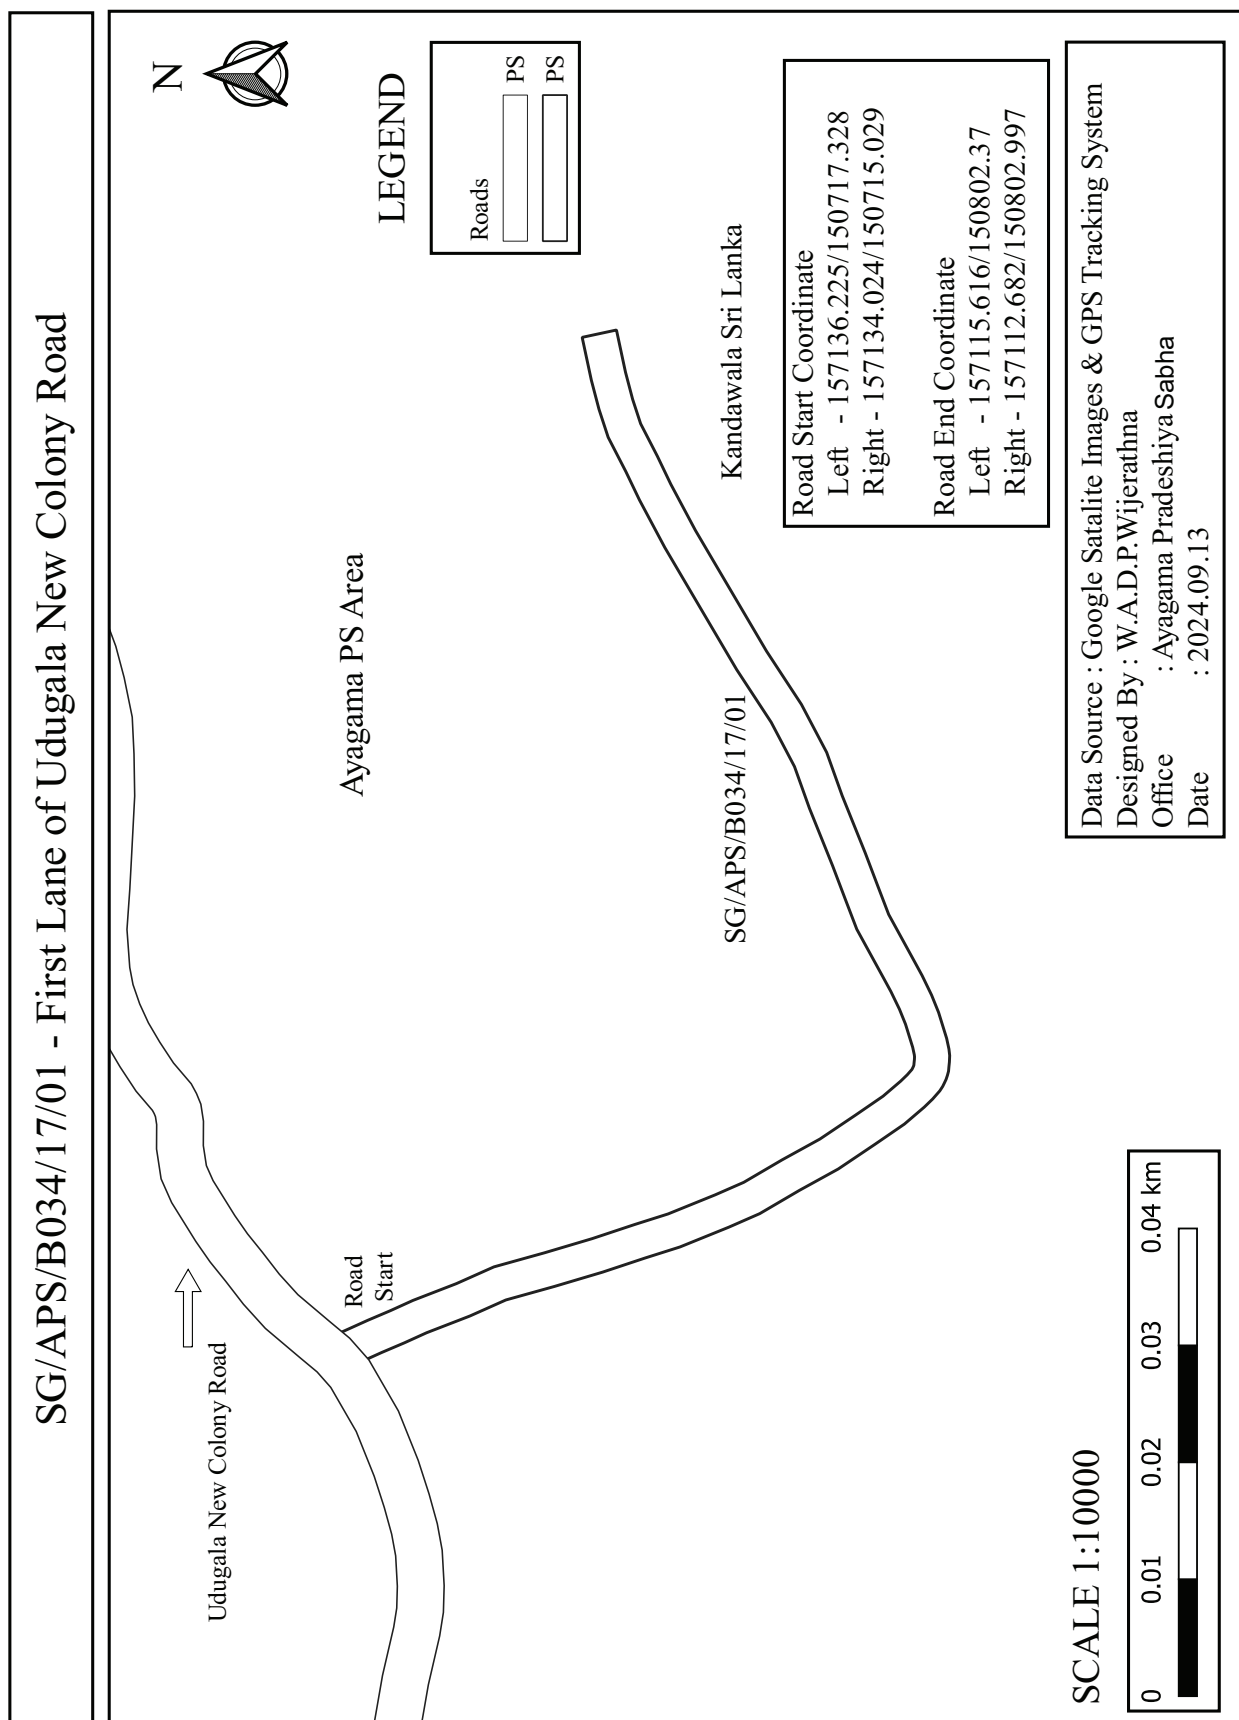


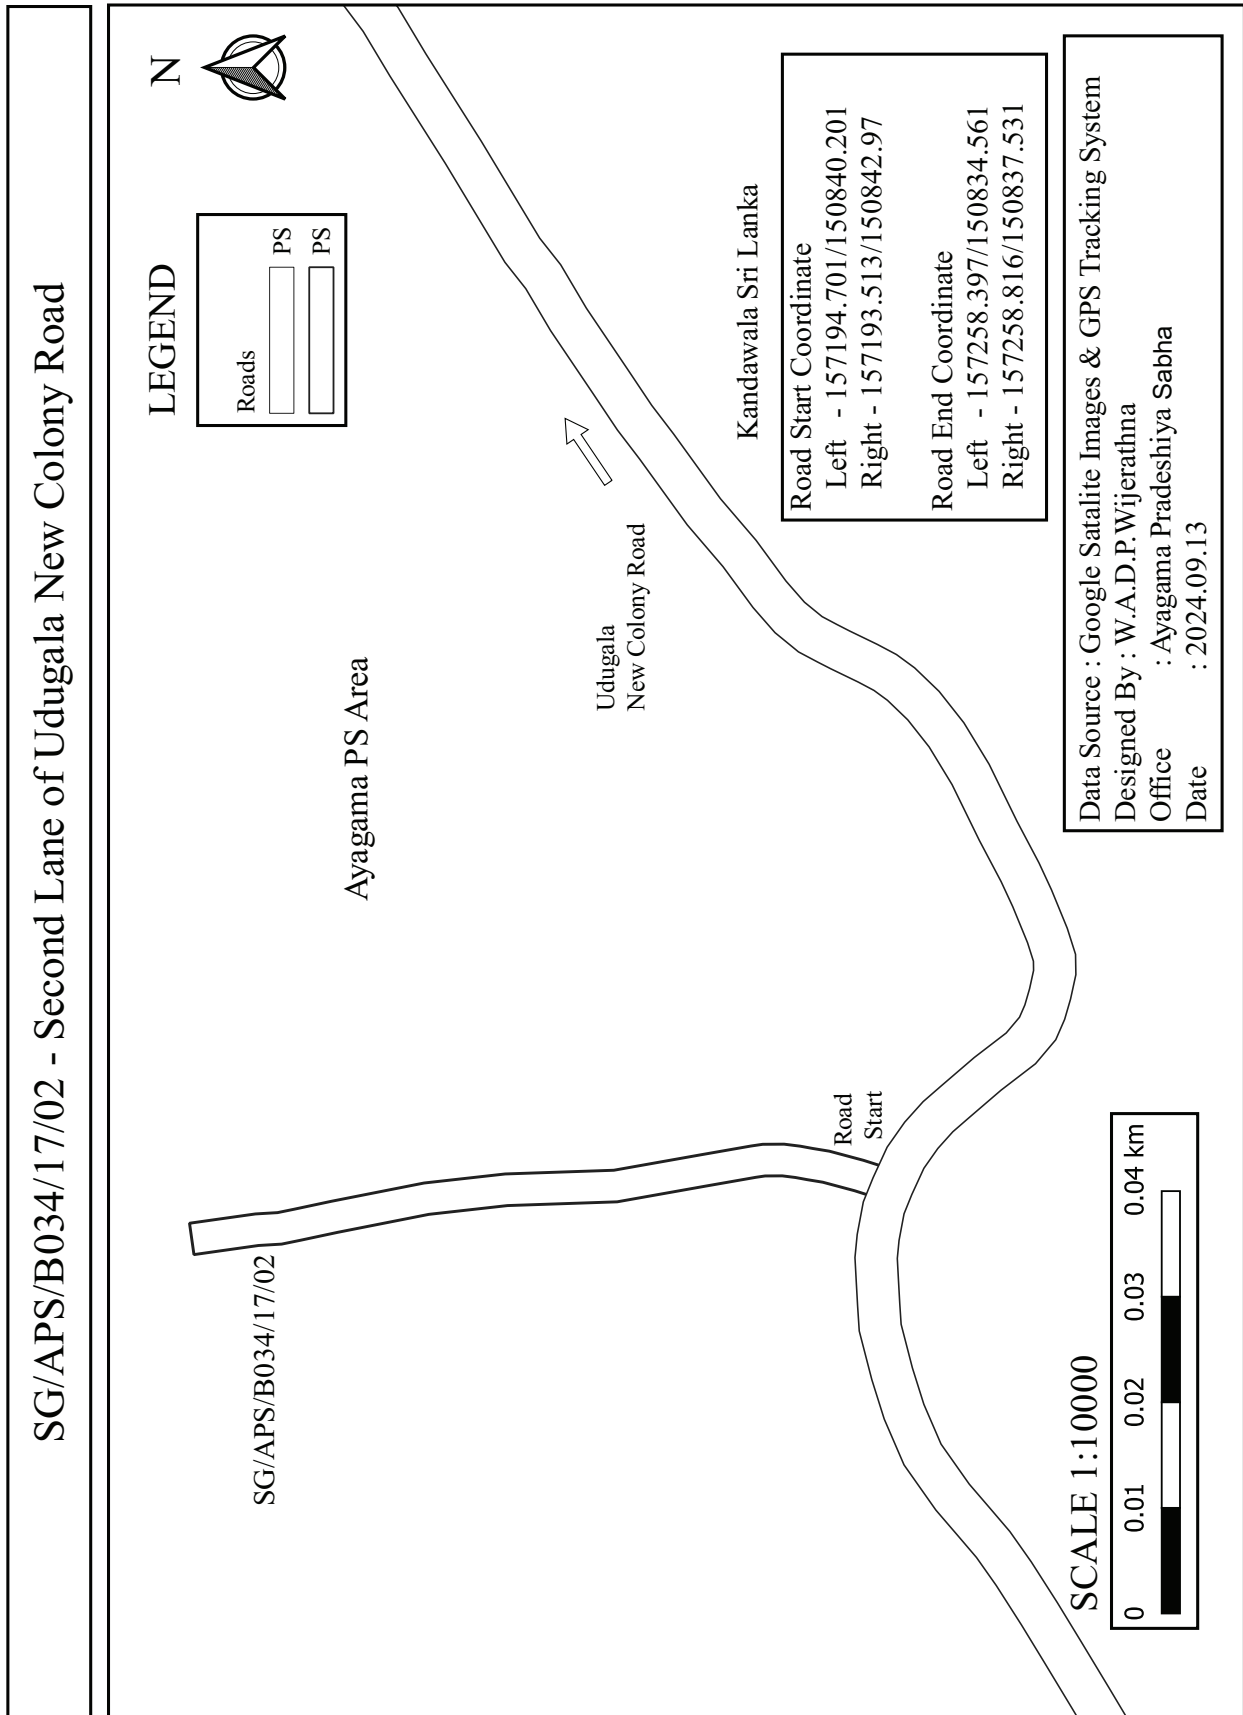


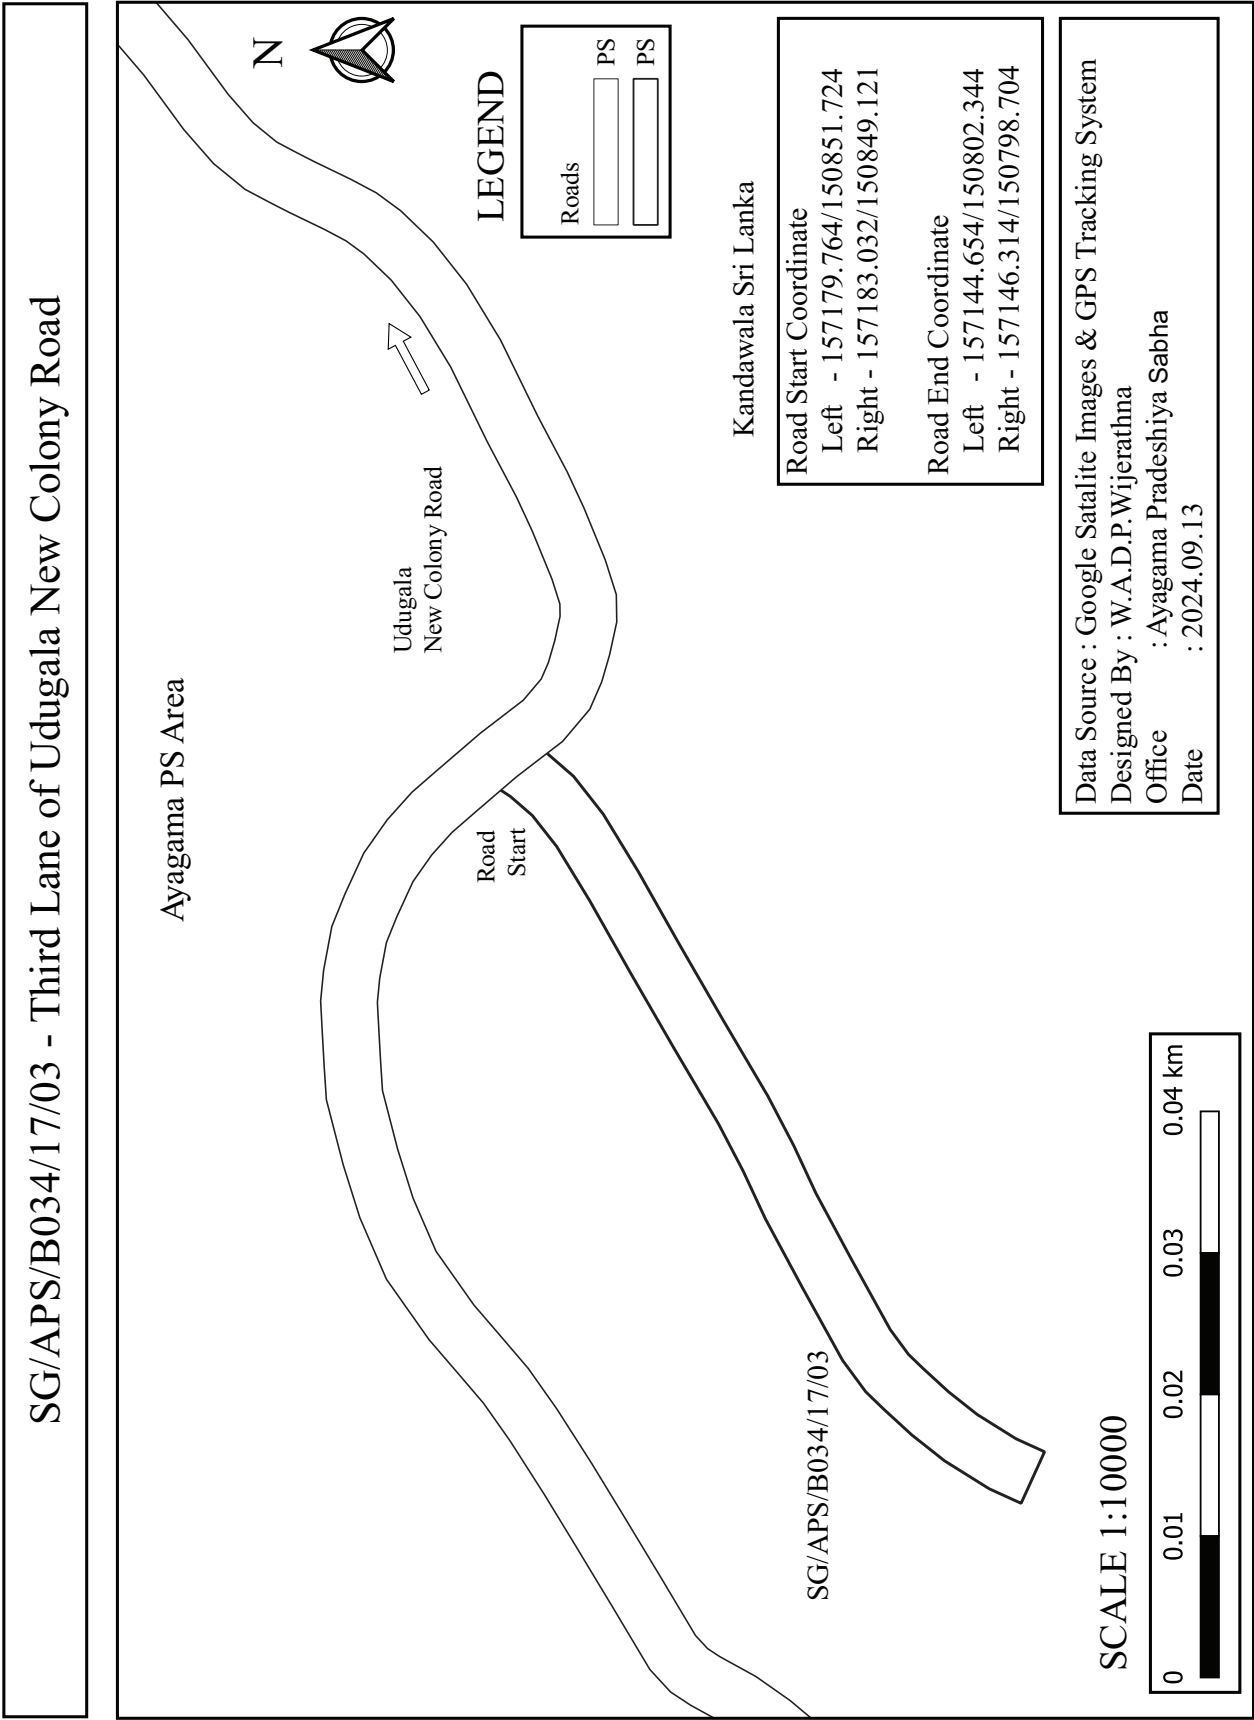


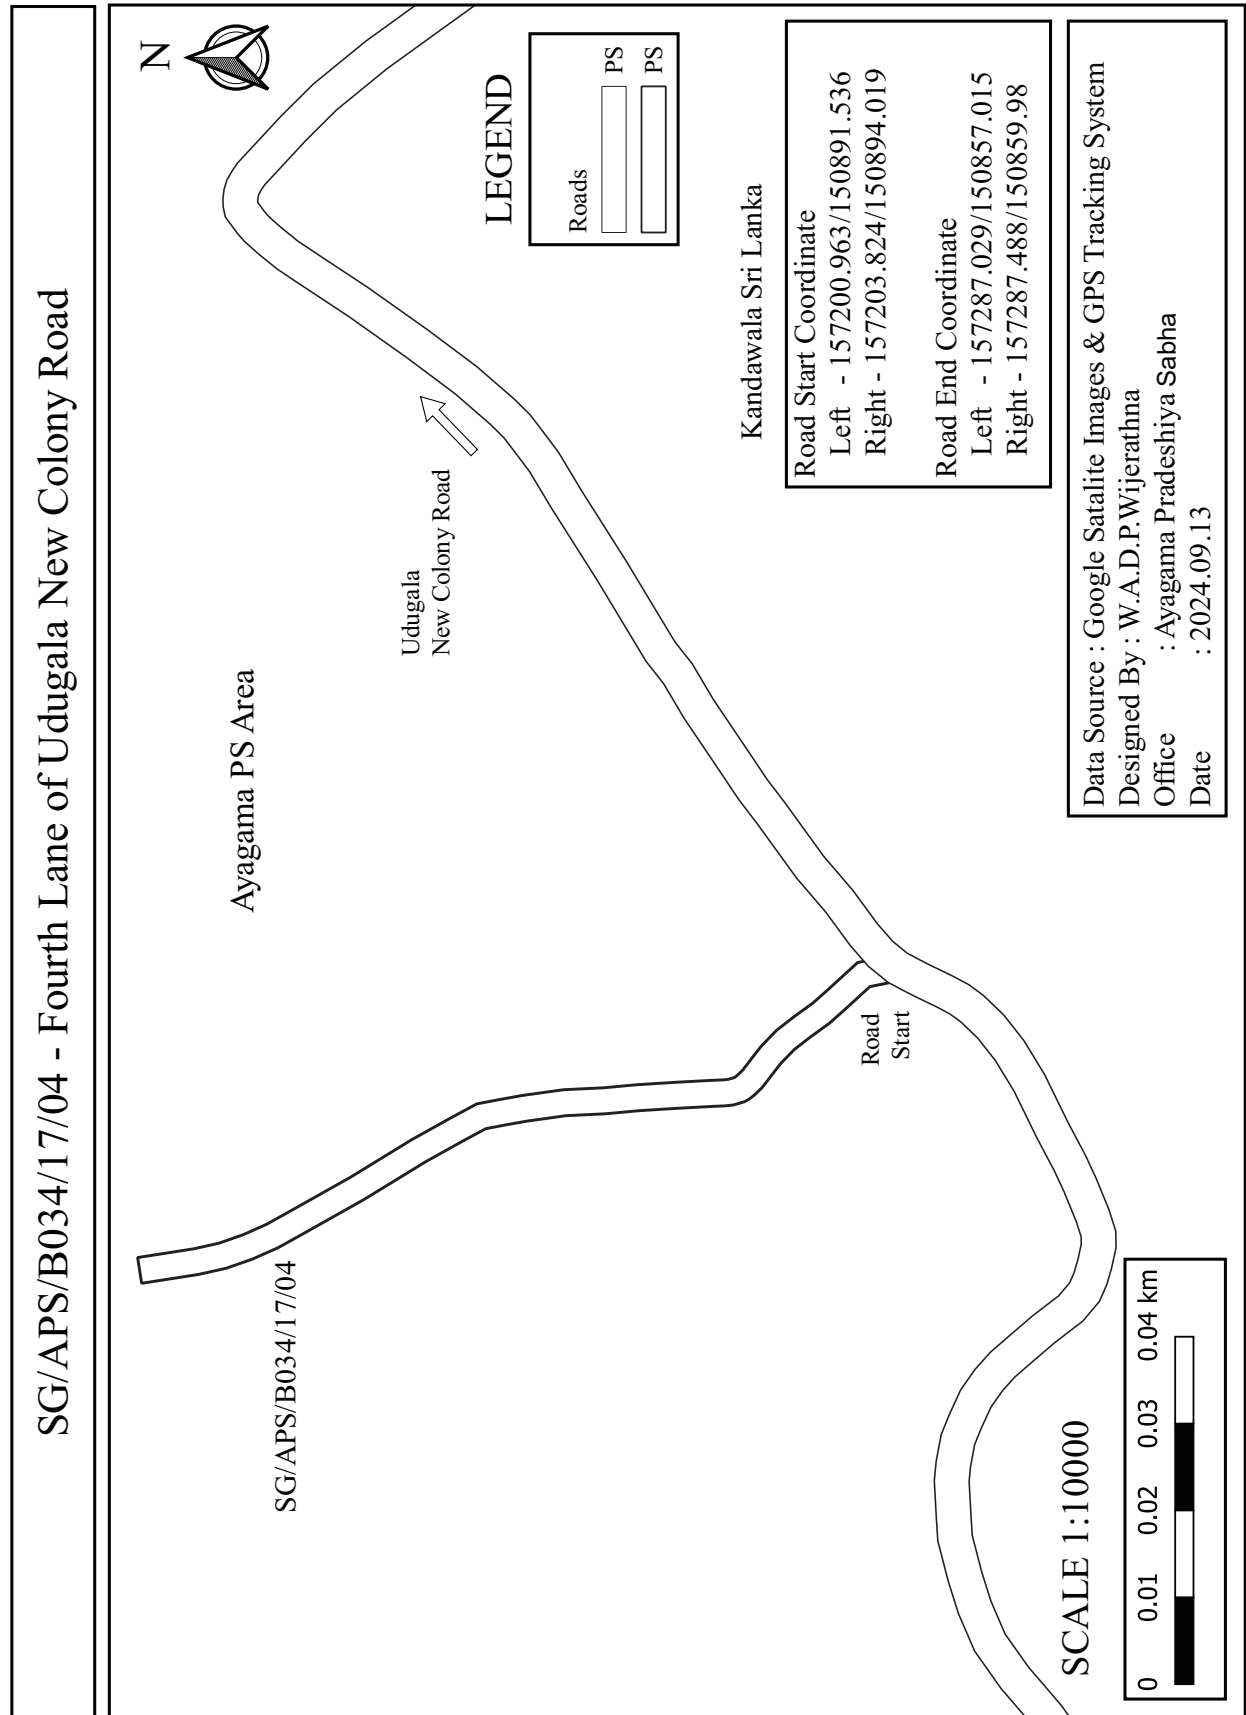


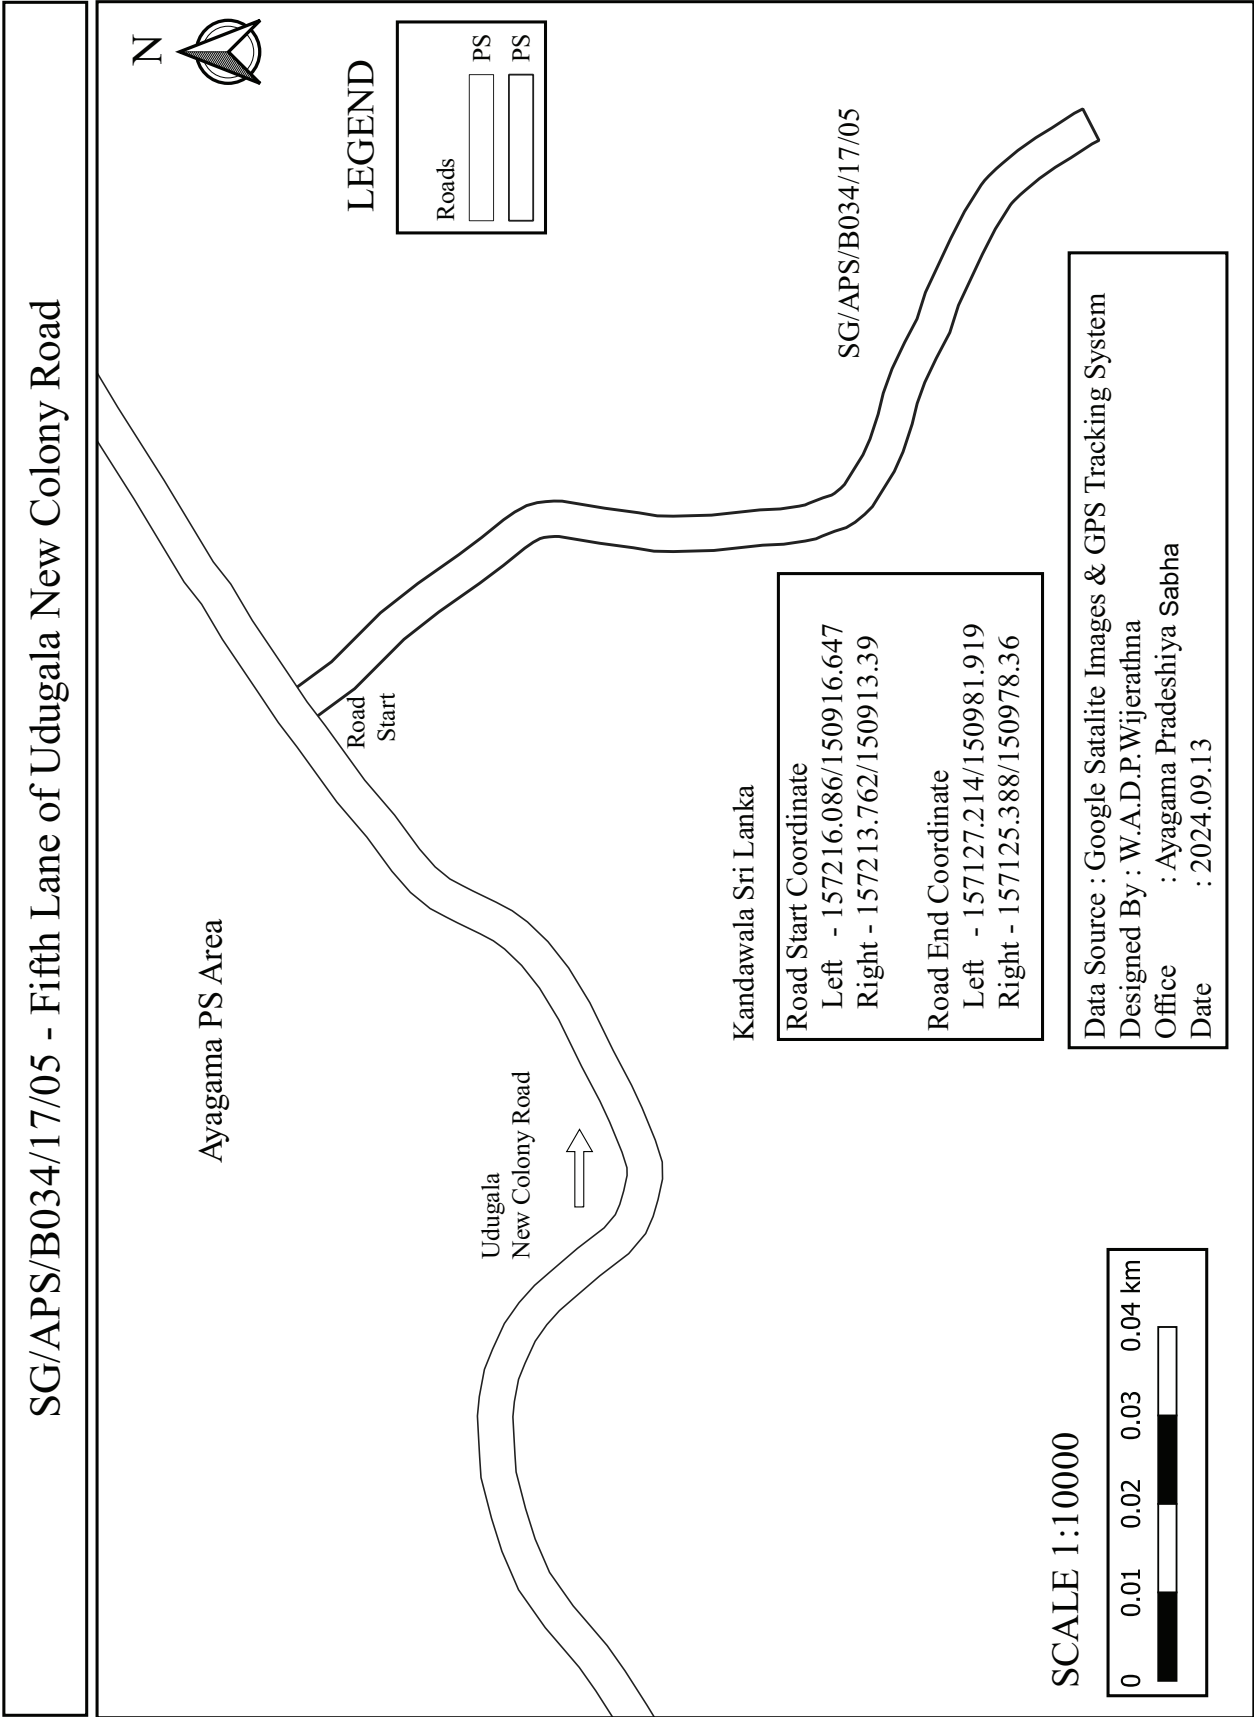


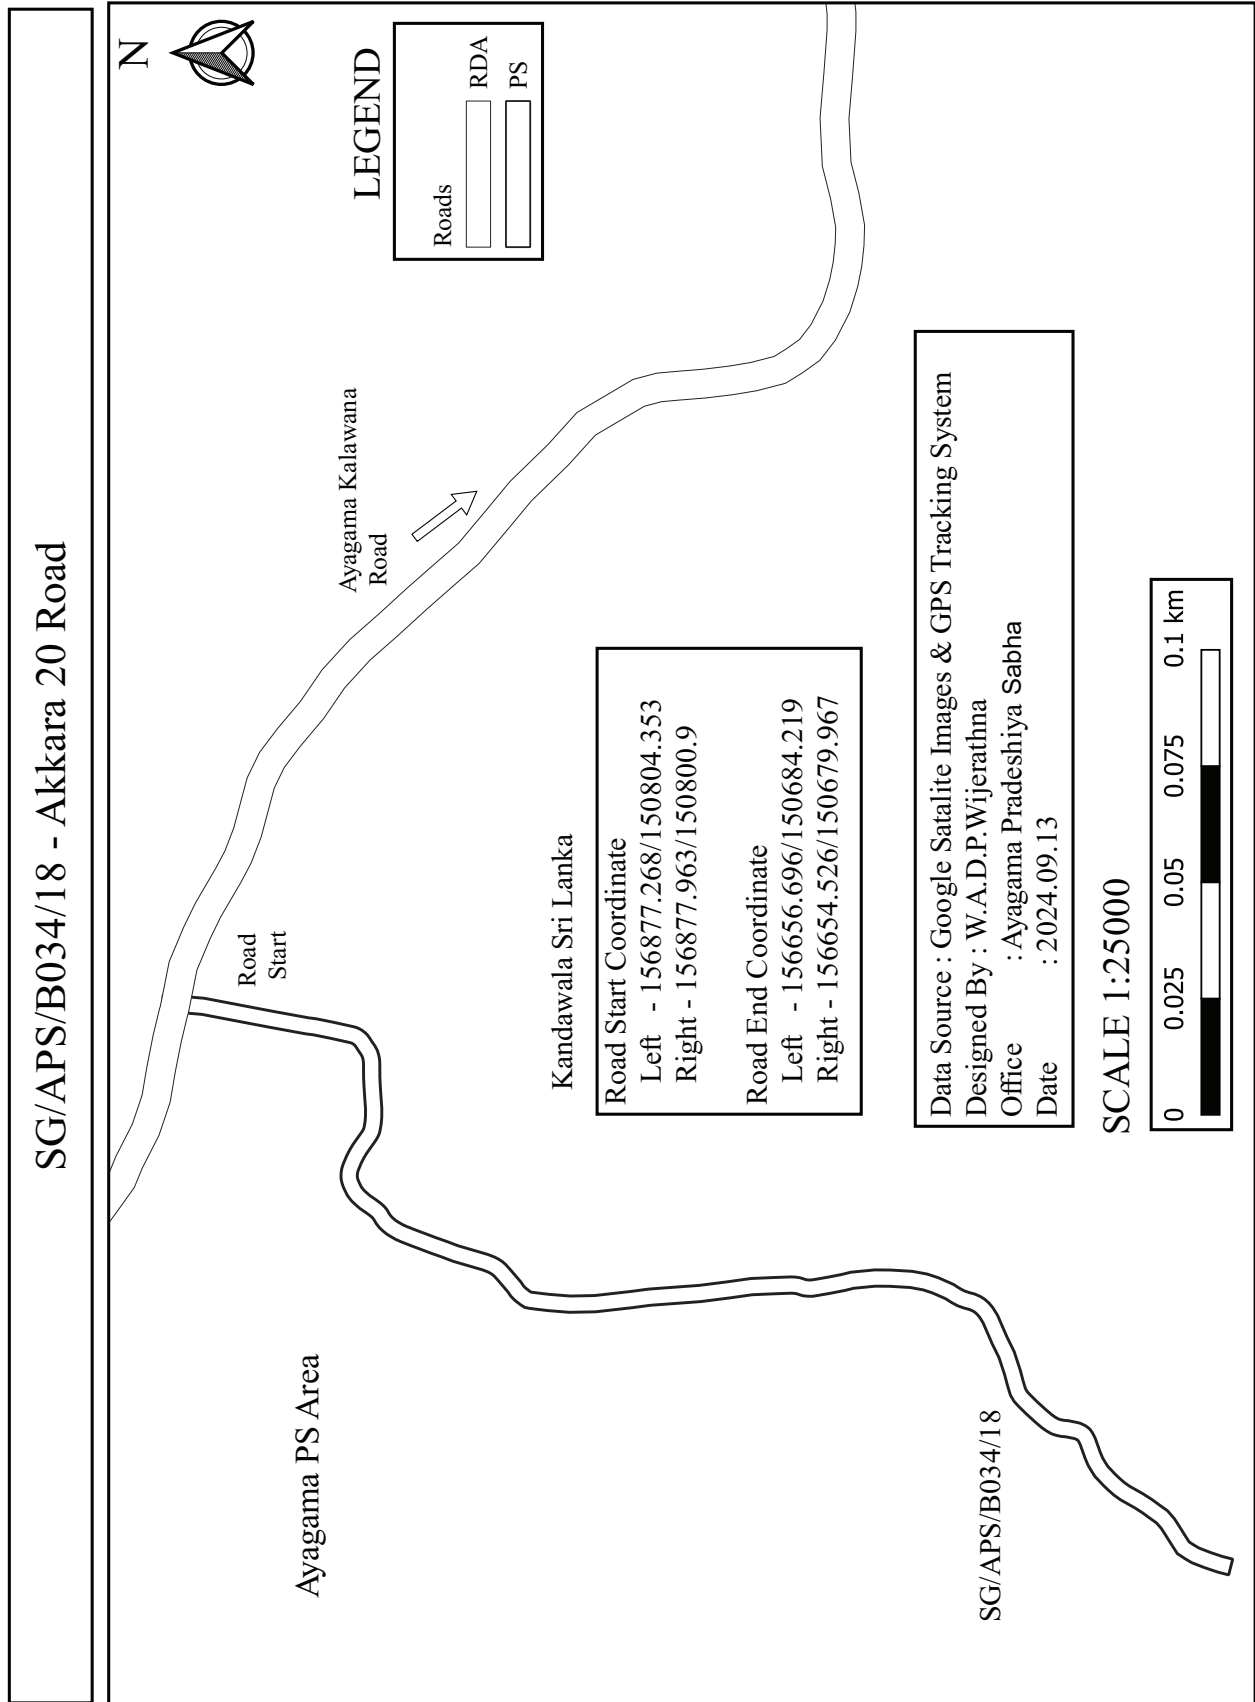


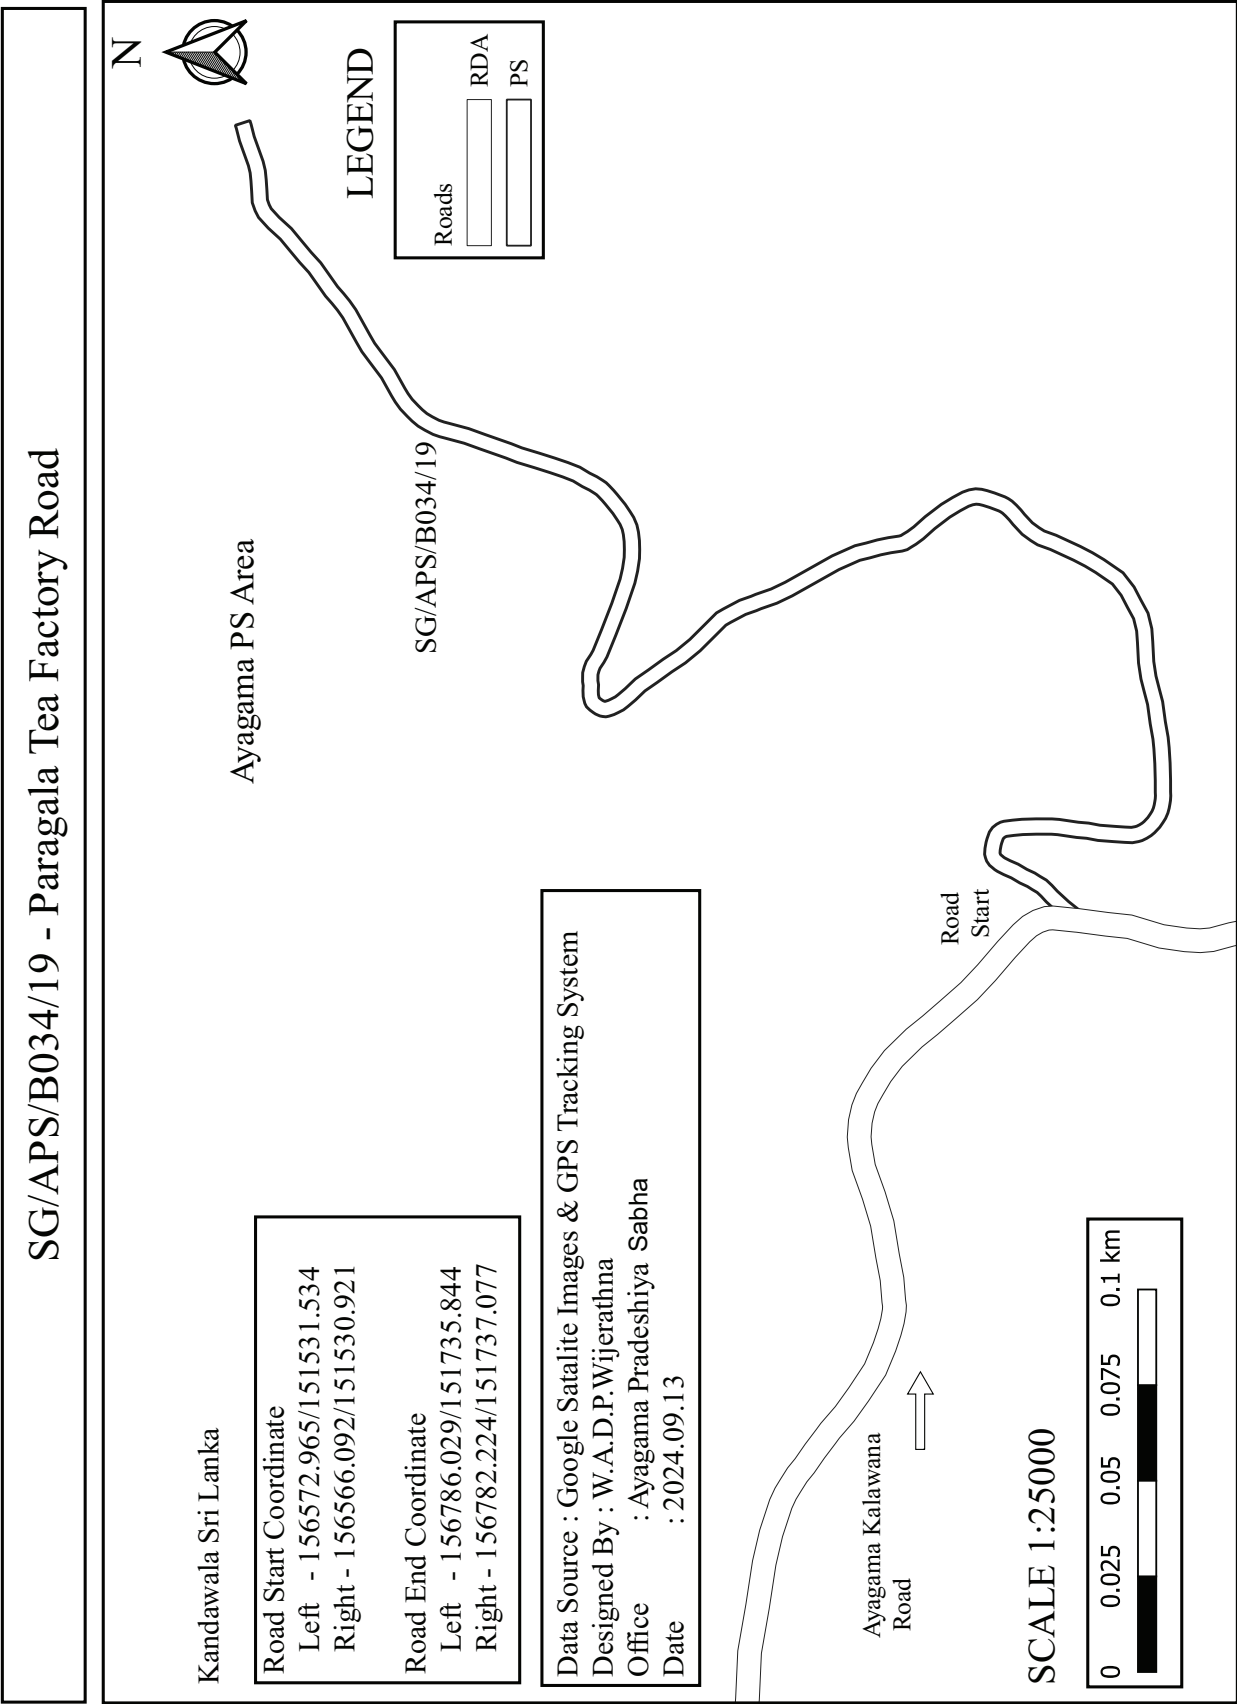


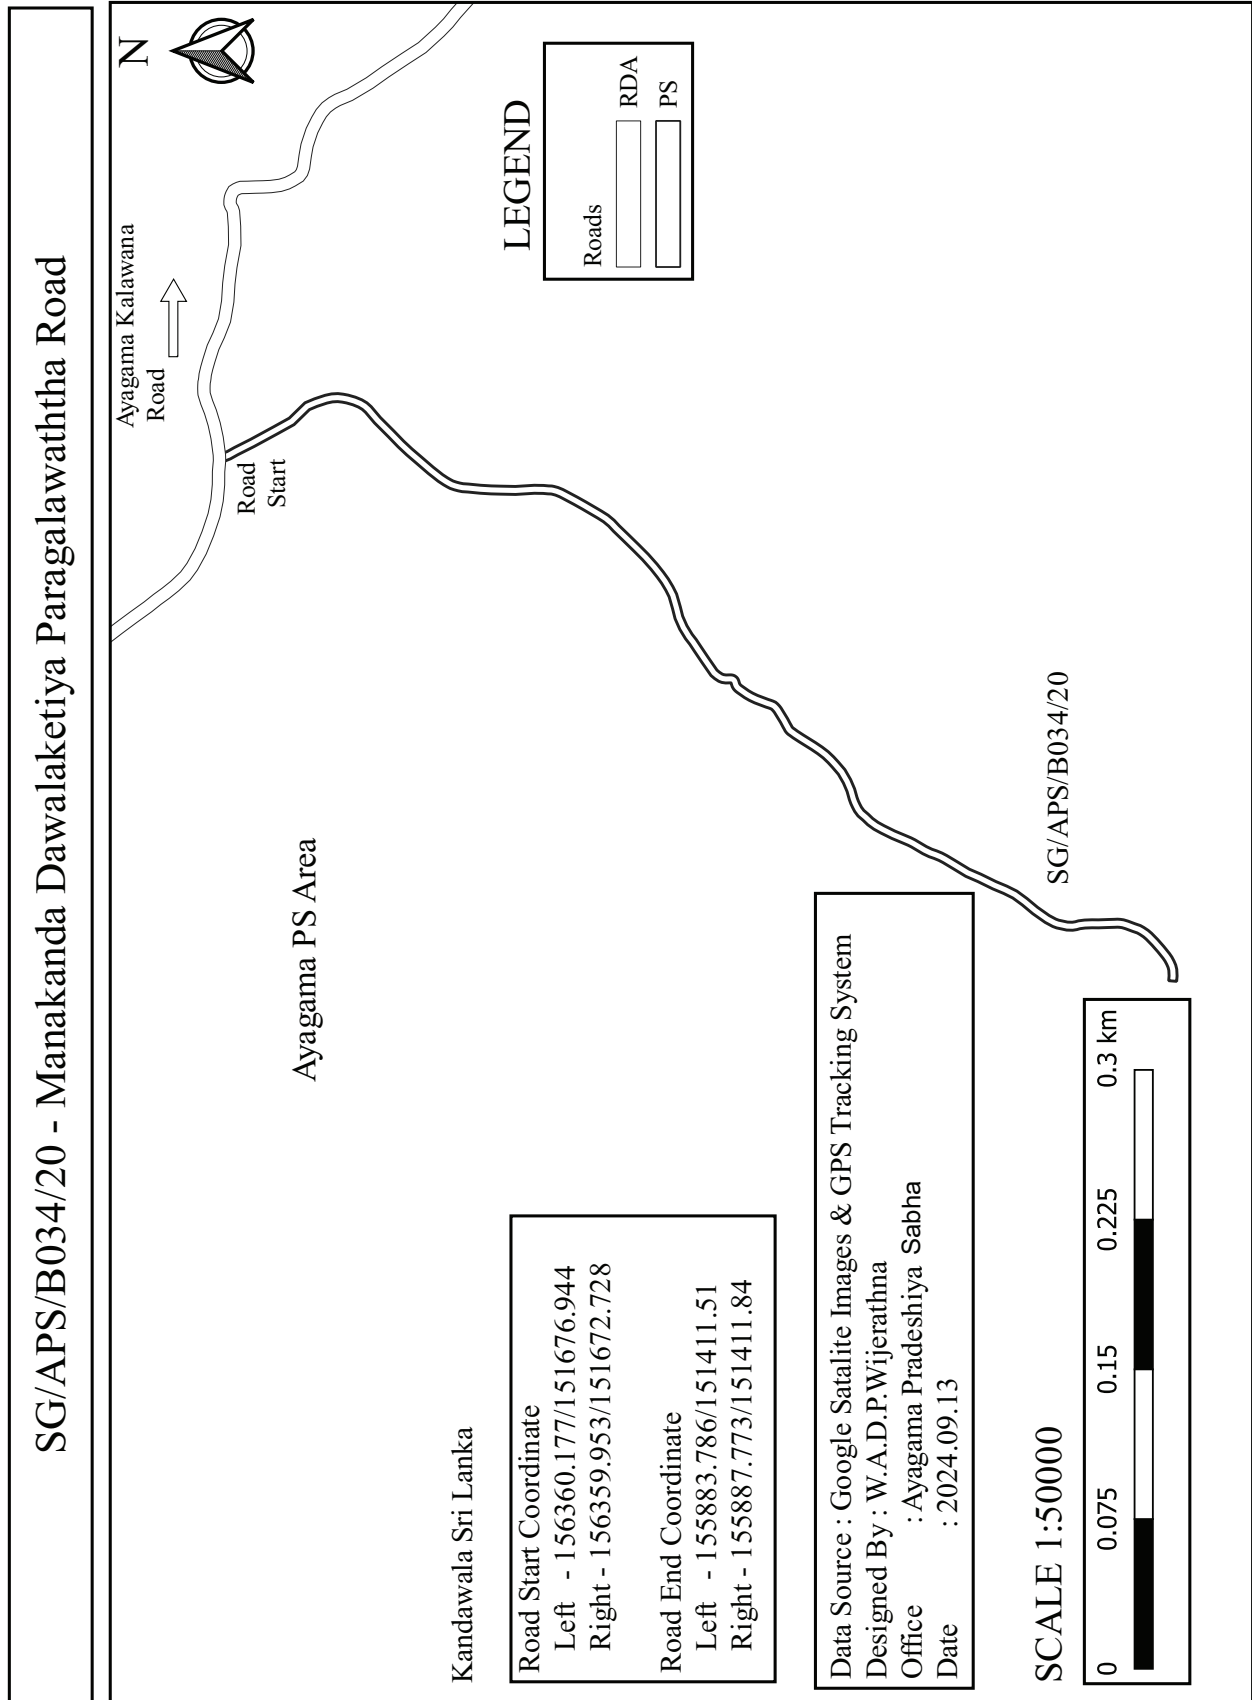


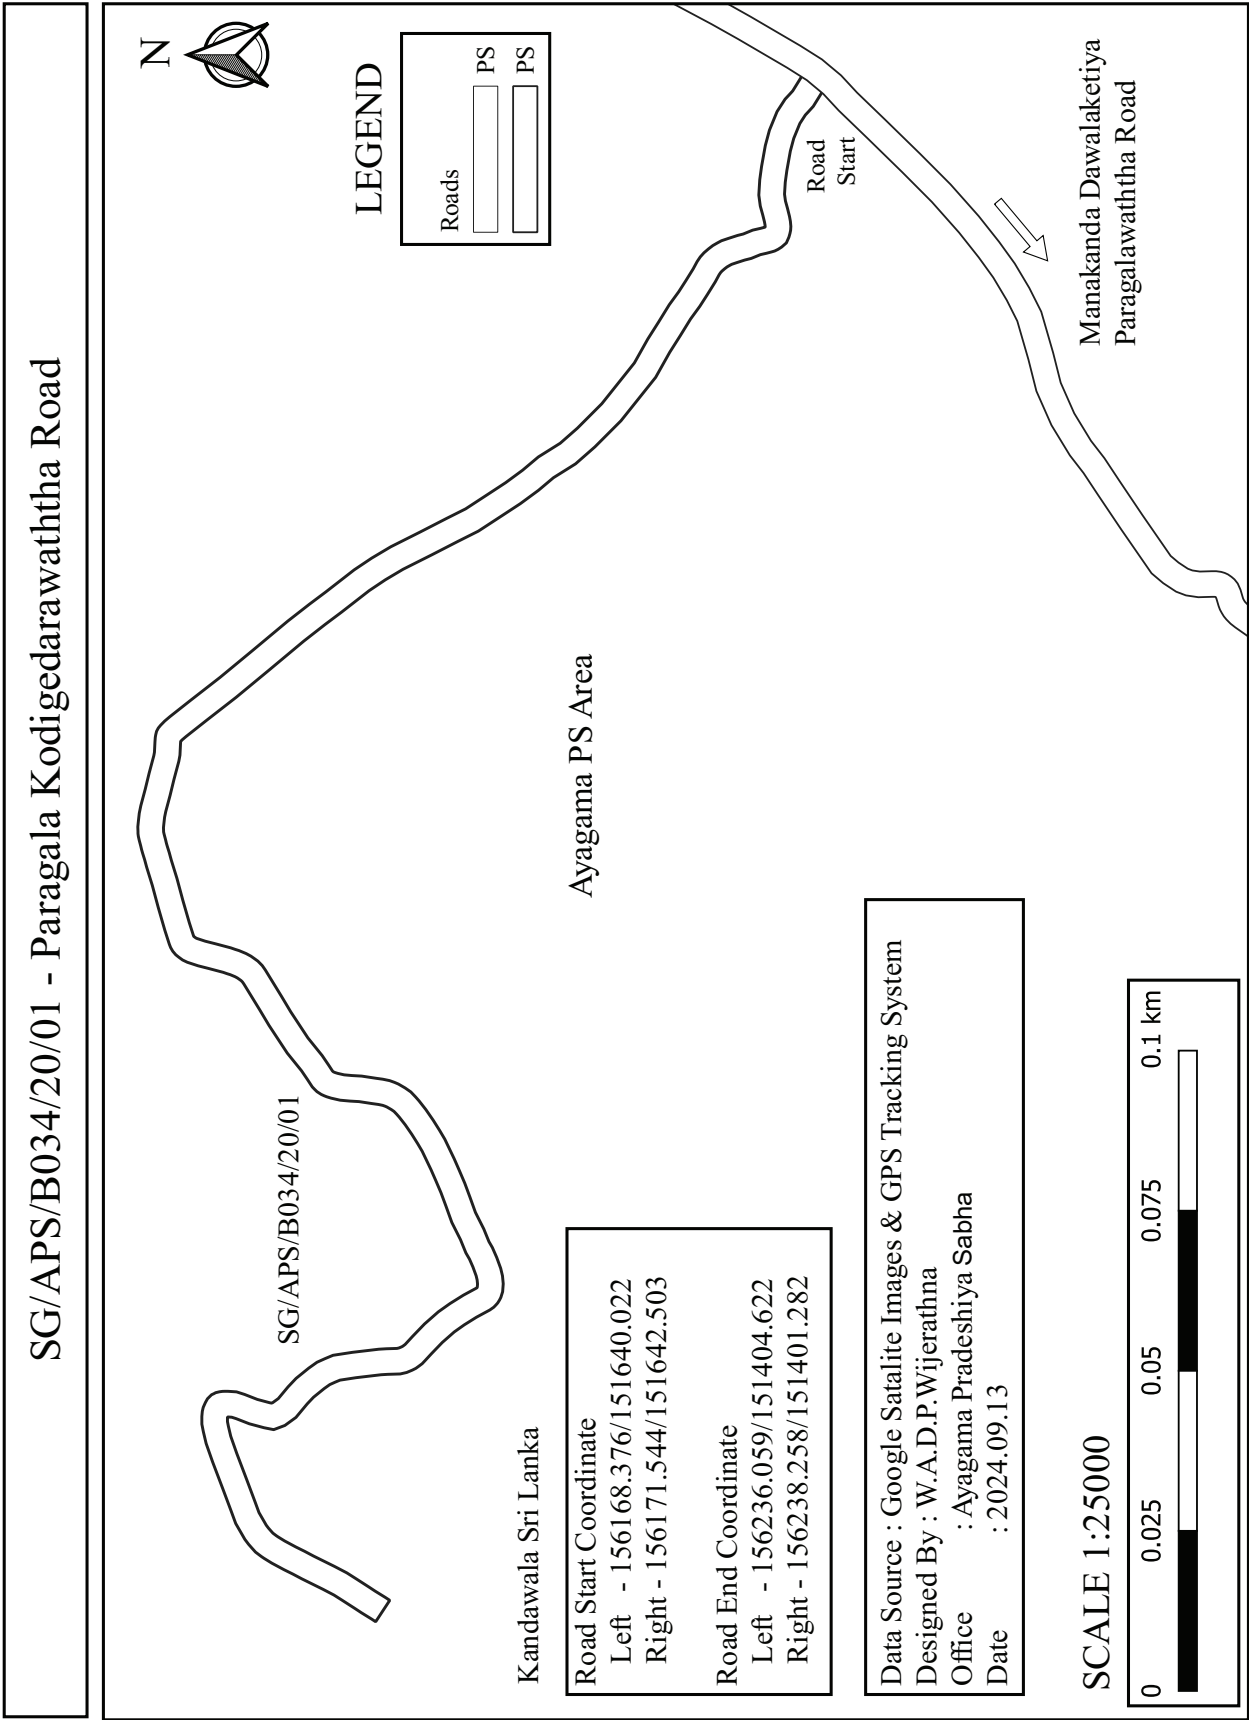

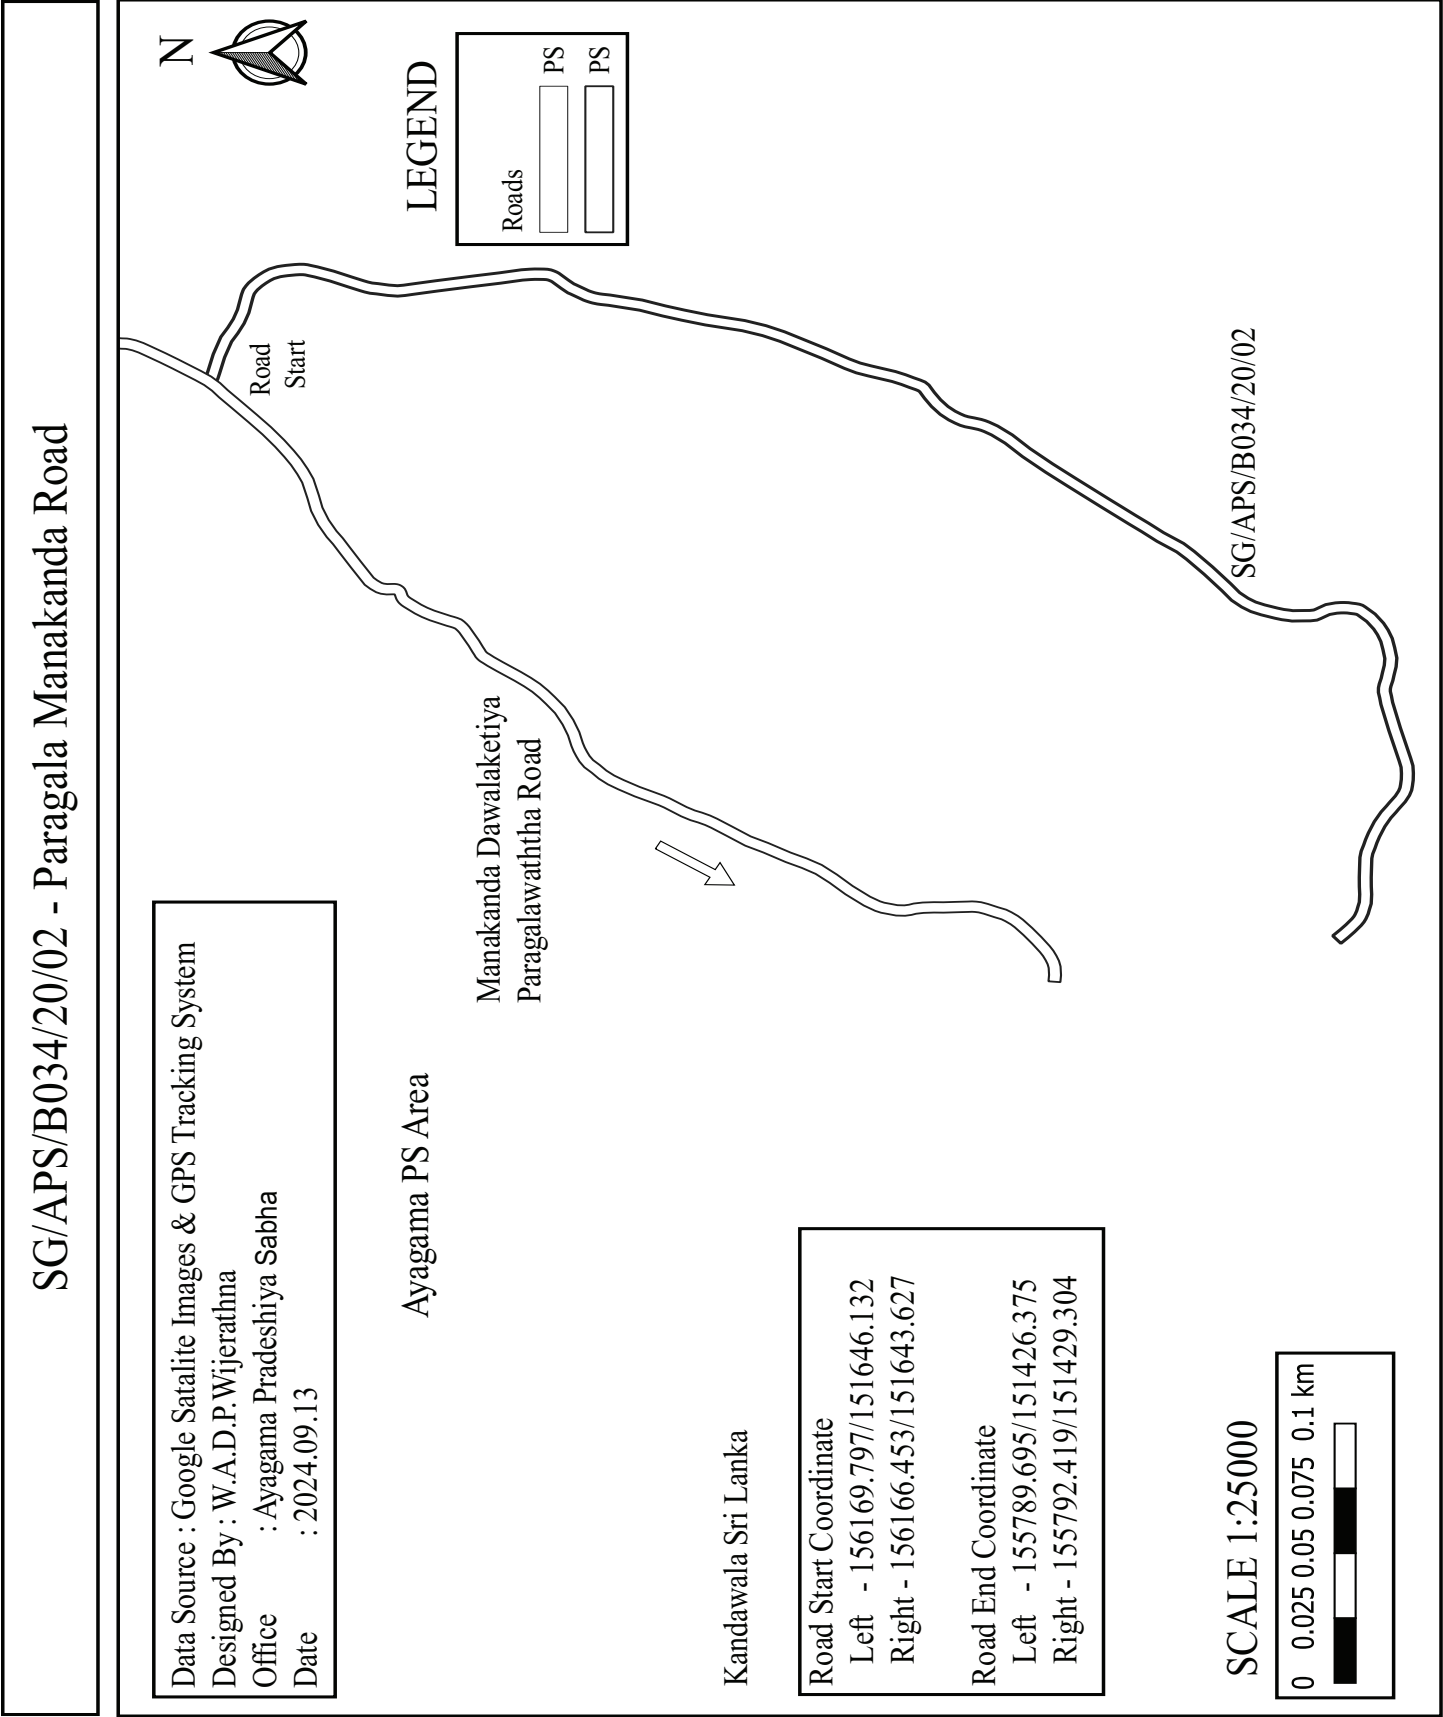


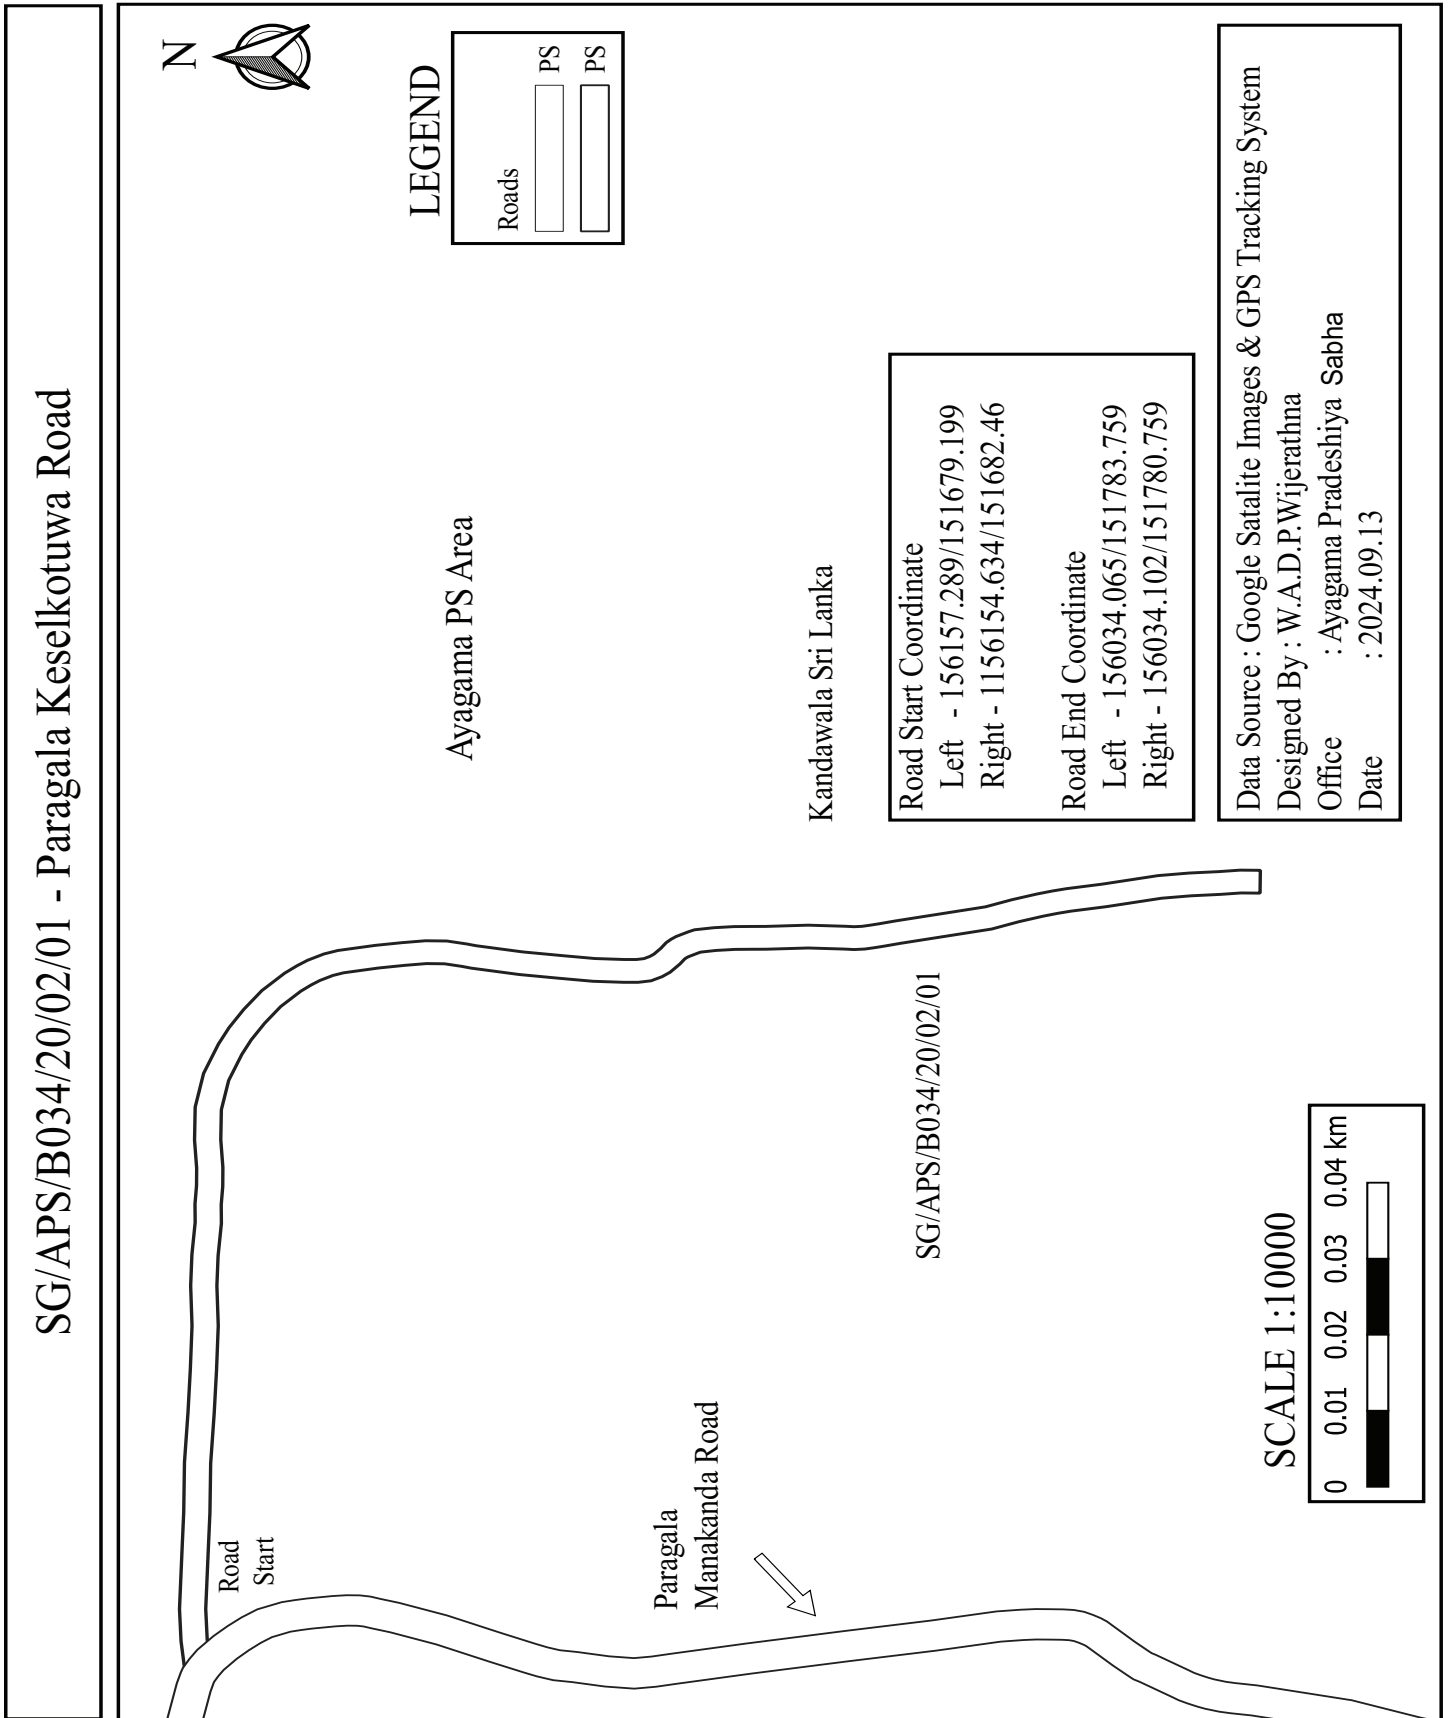


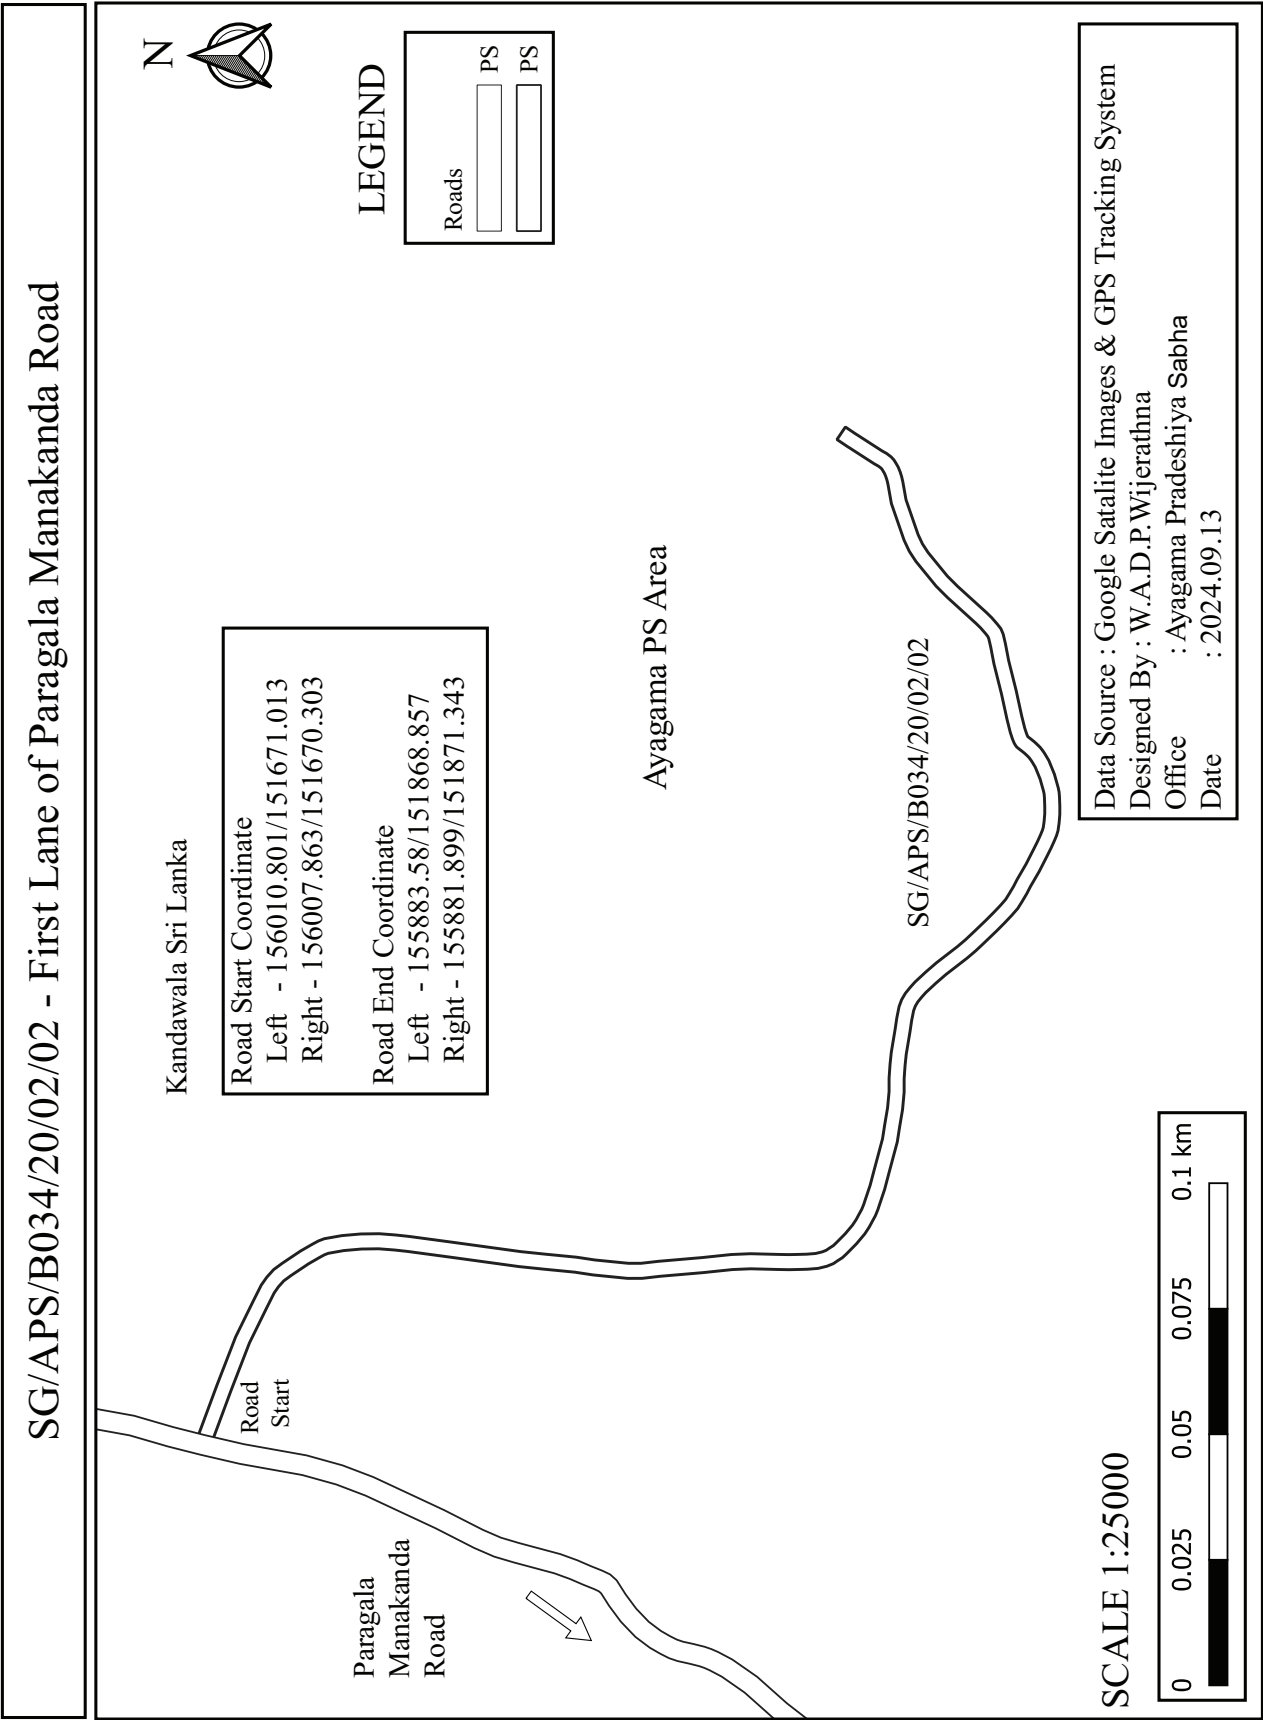


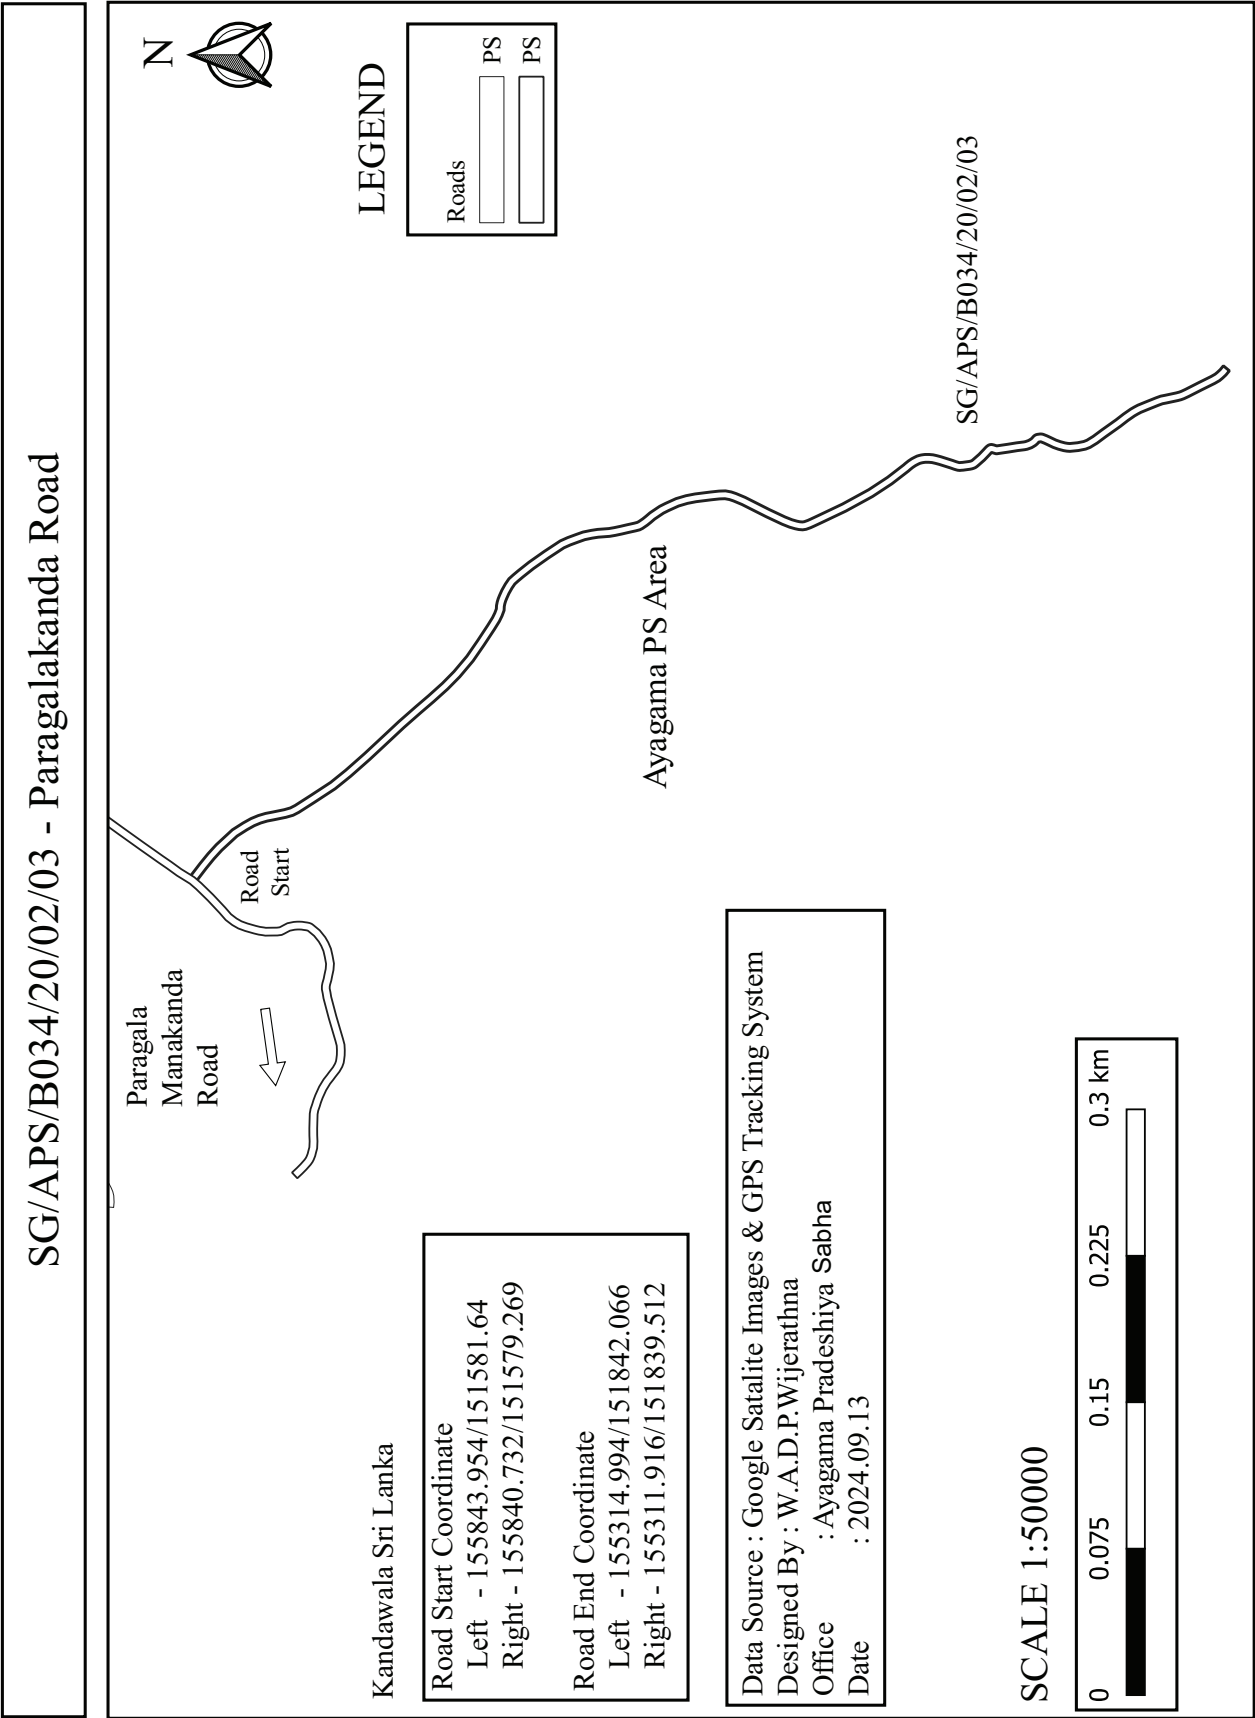


SG/APS/B034/20/02/04 - Manakanda Paragalakanda Road

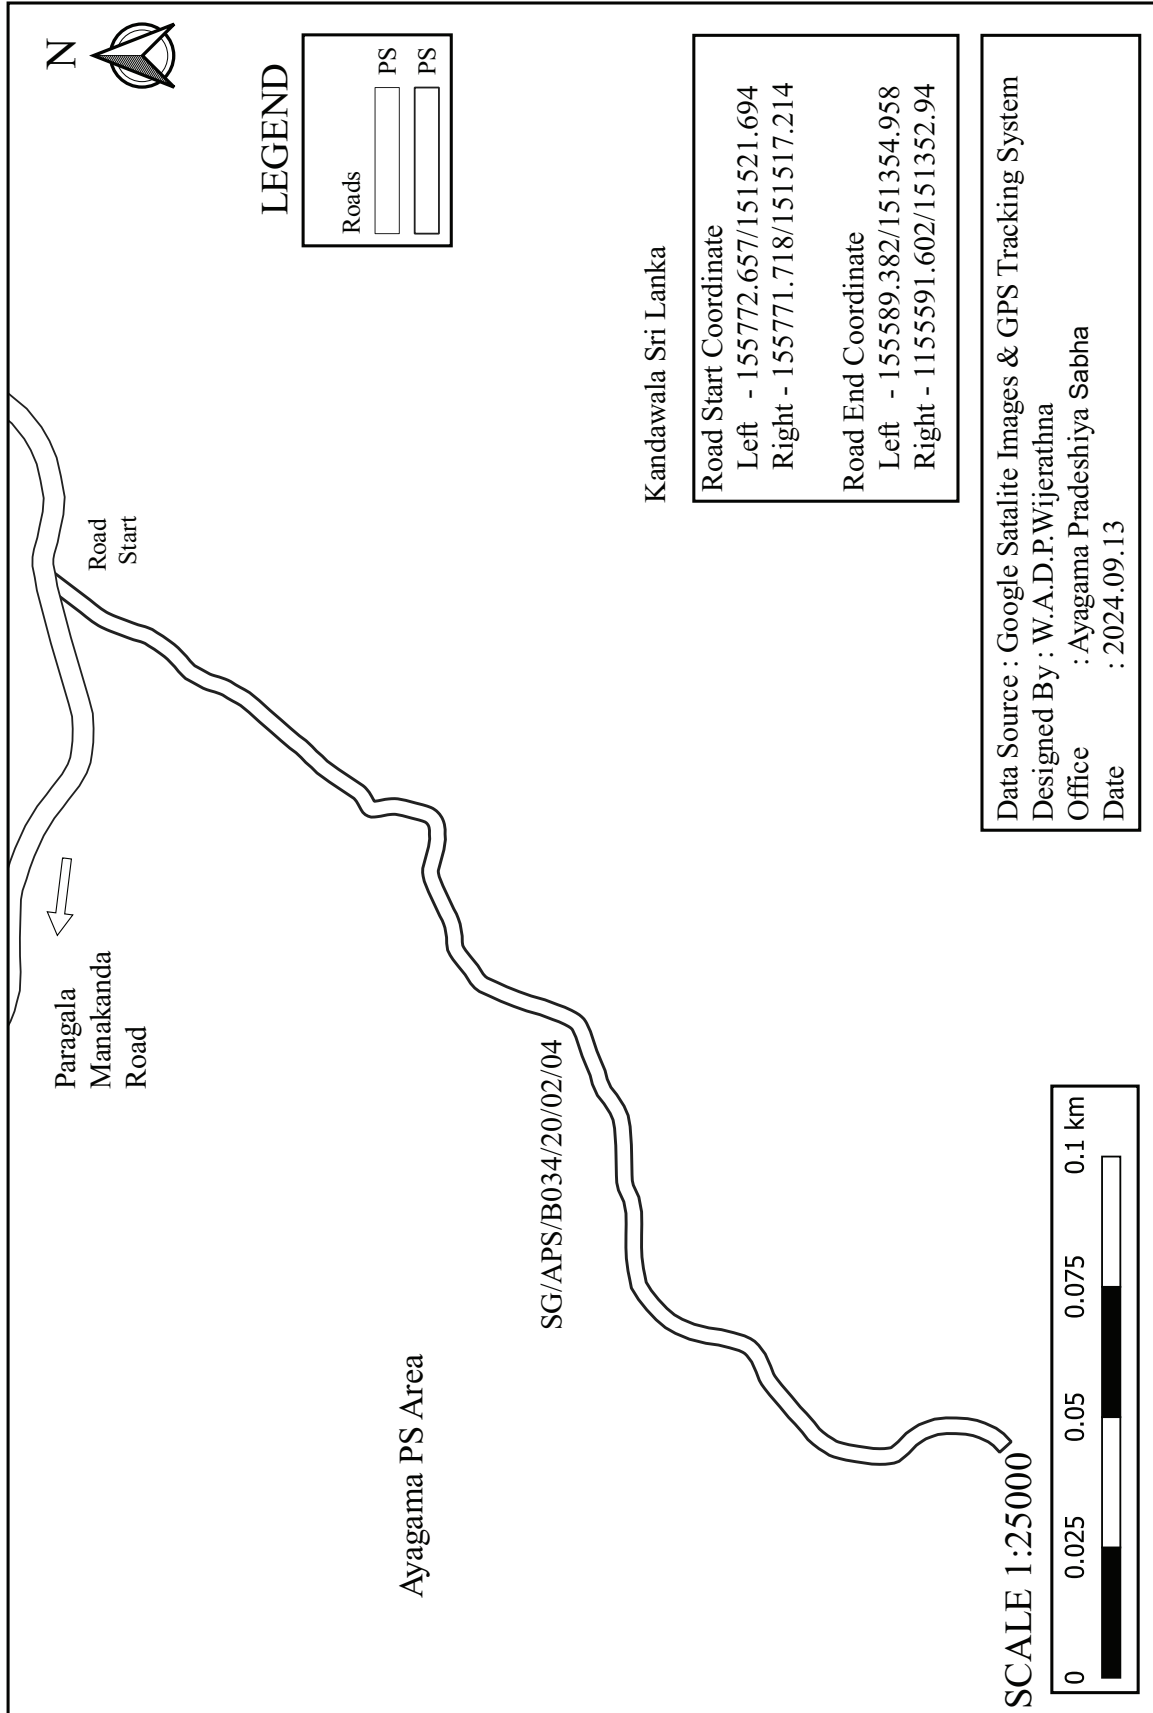


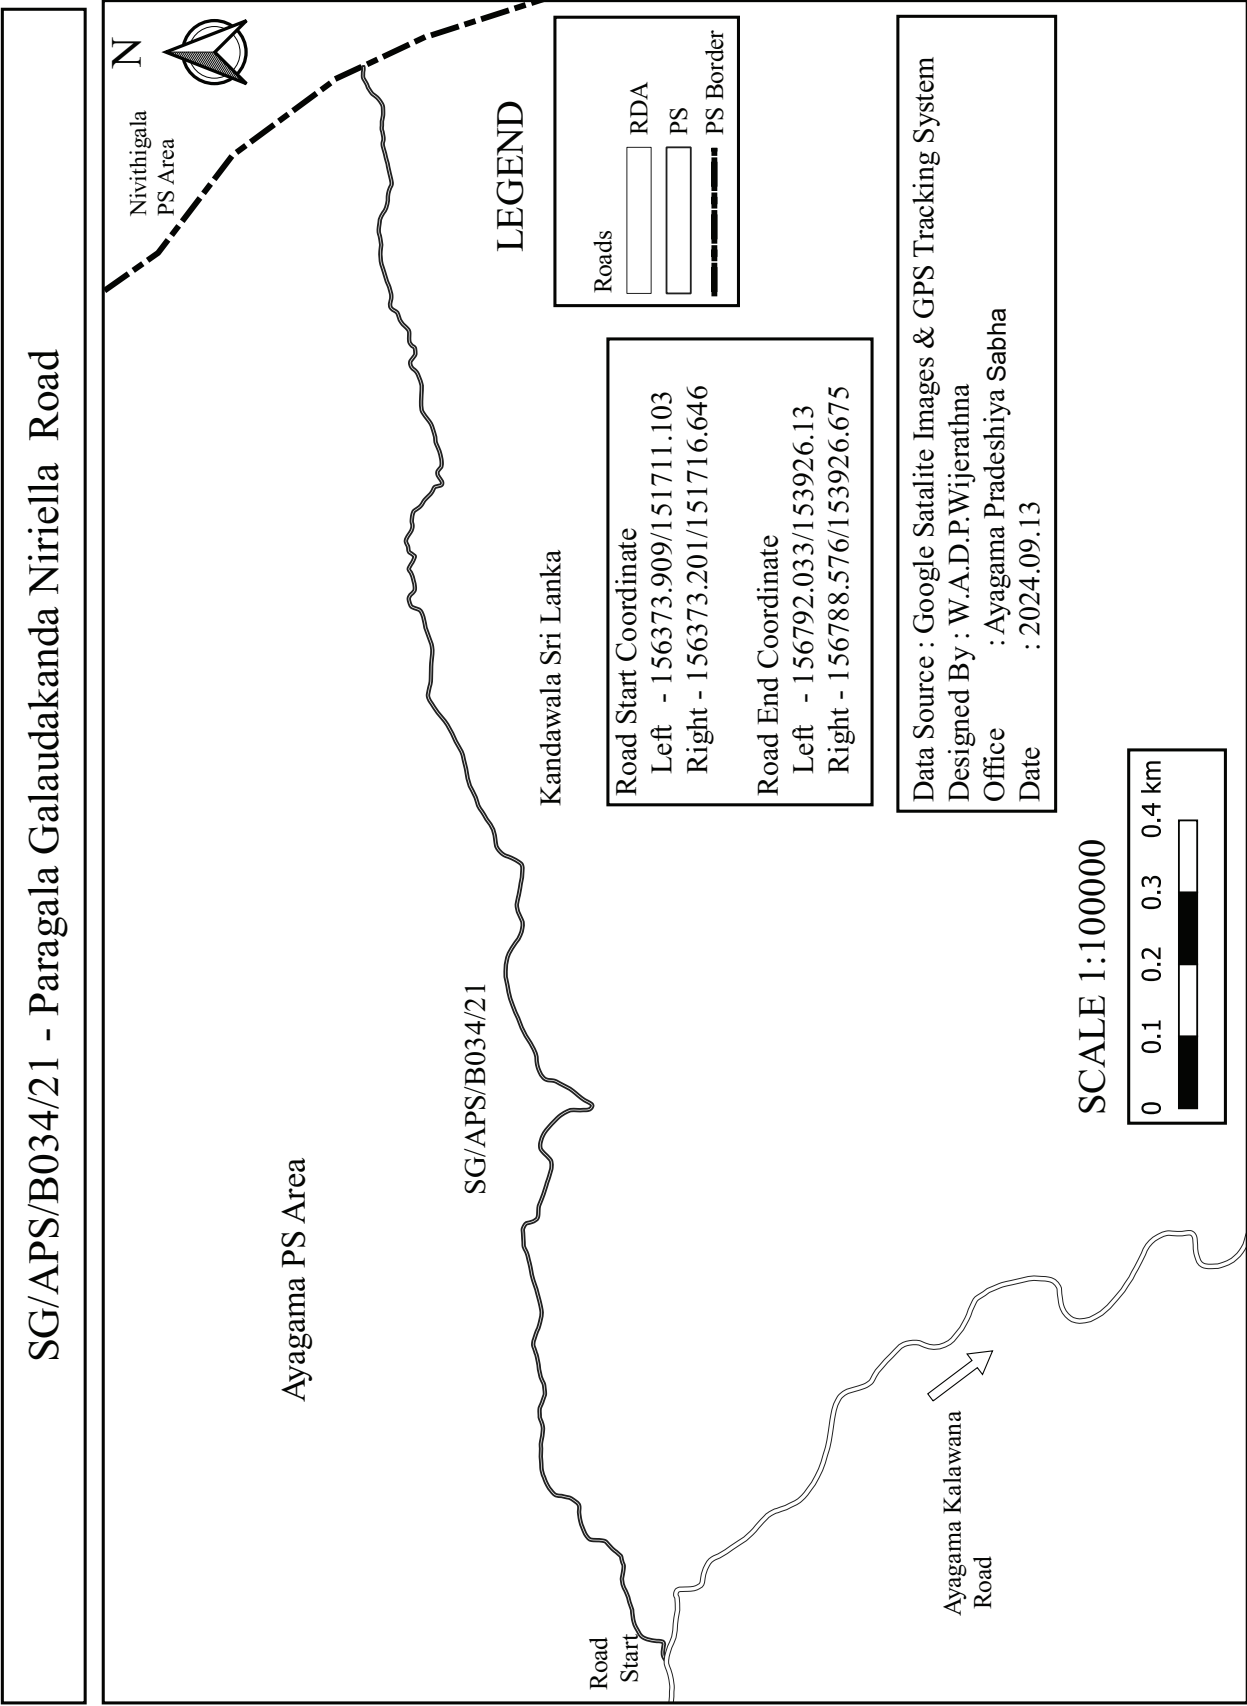


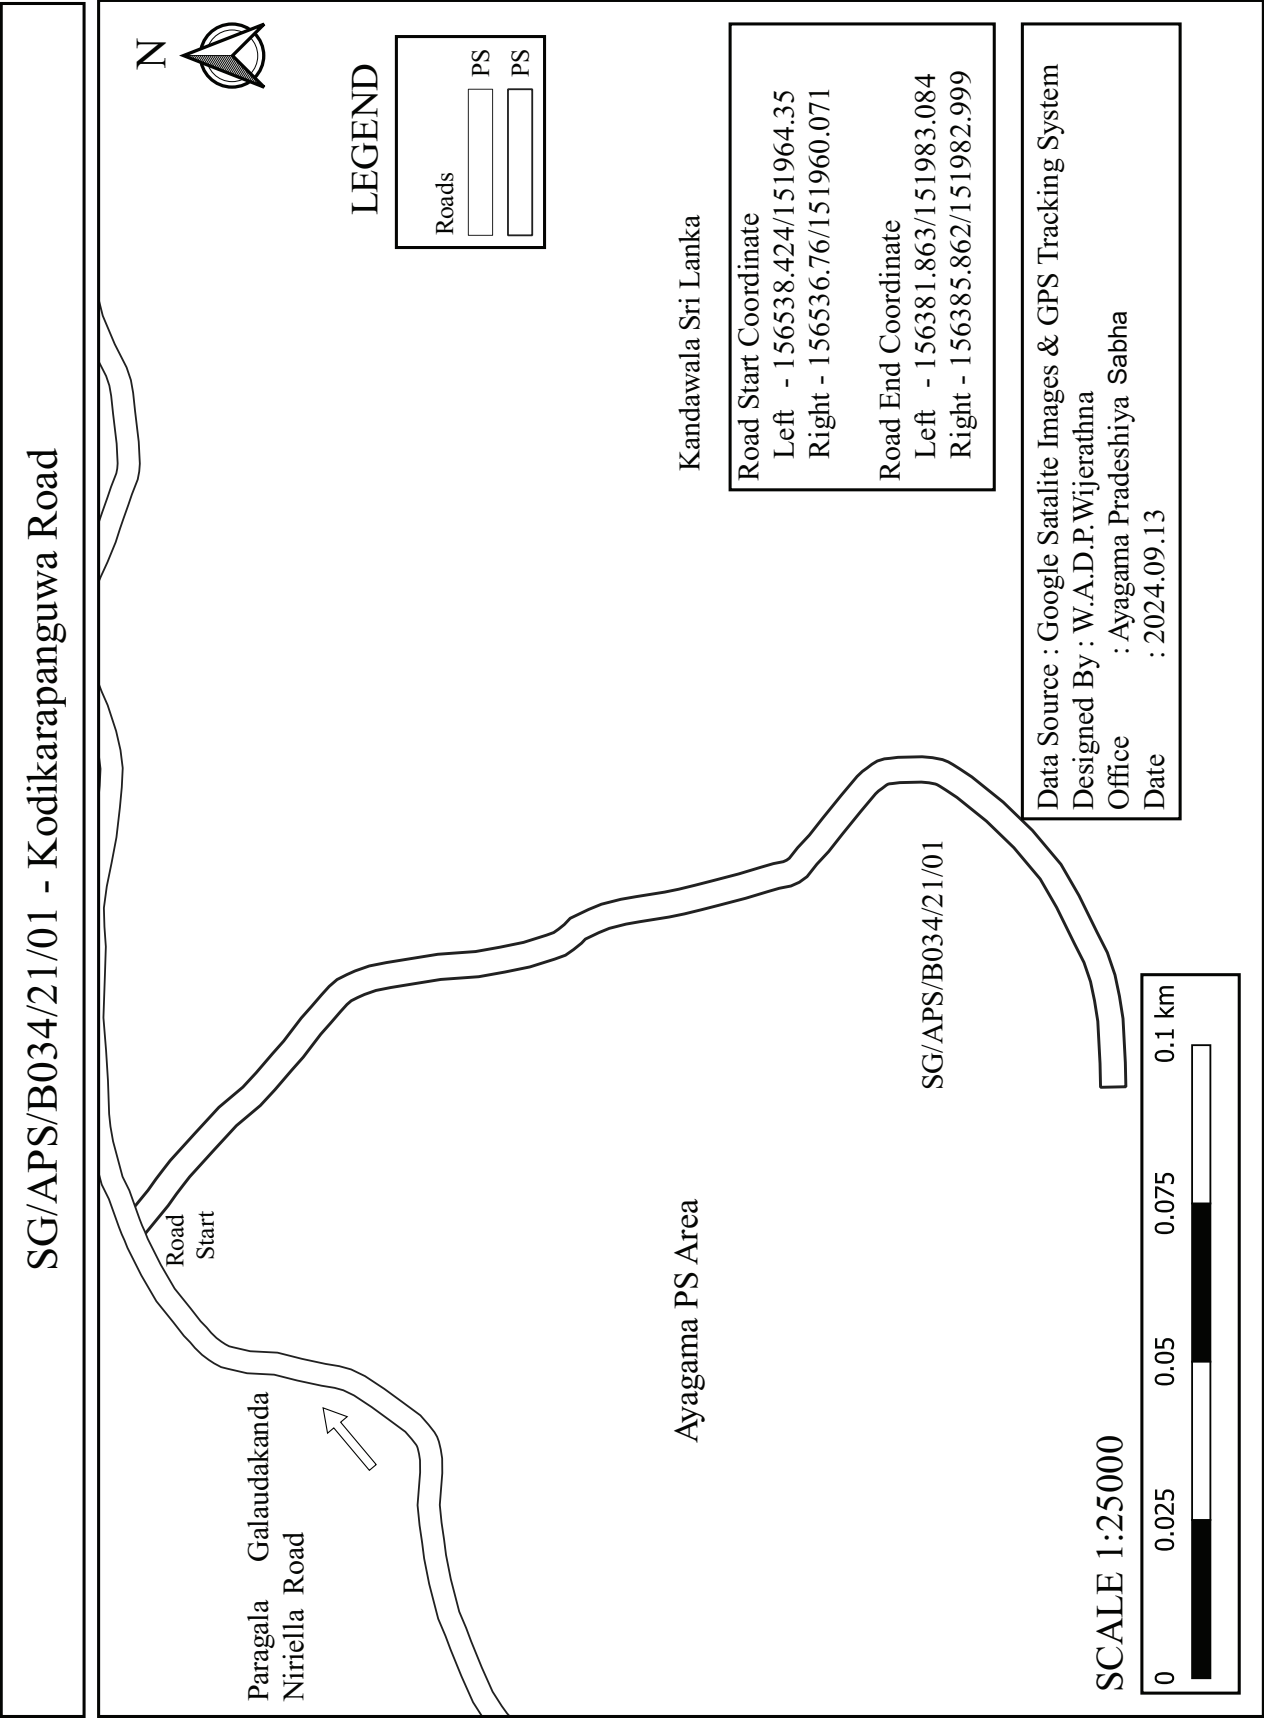


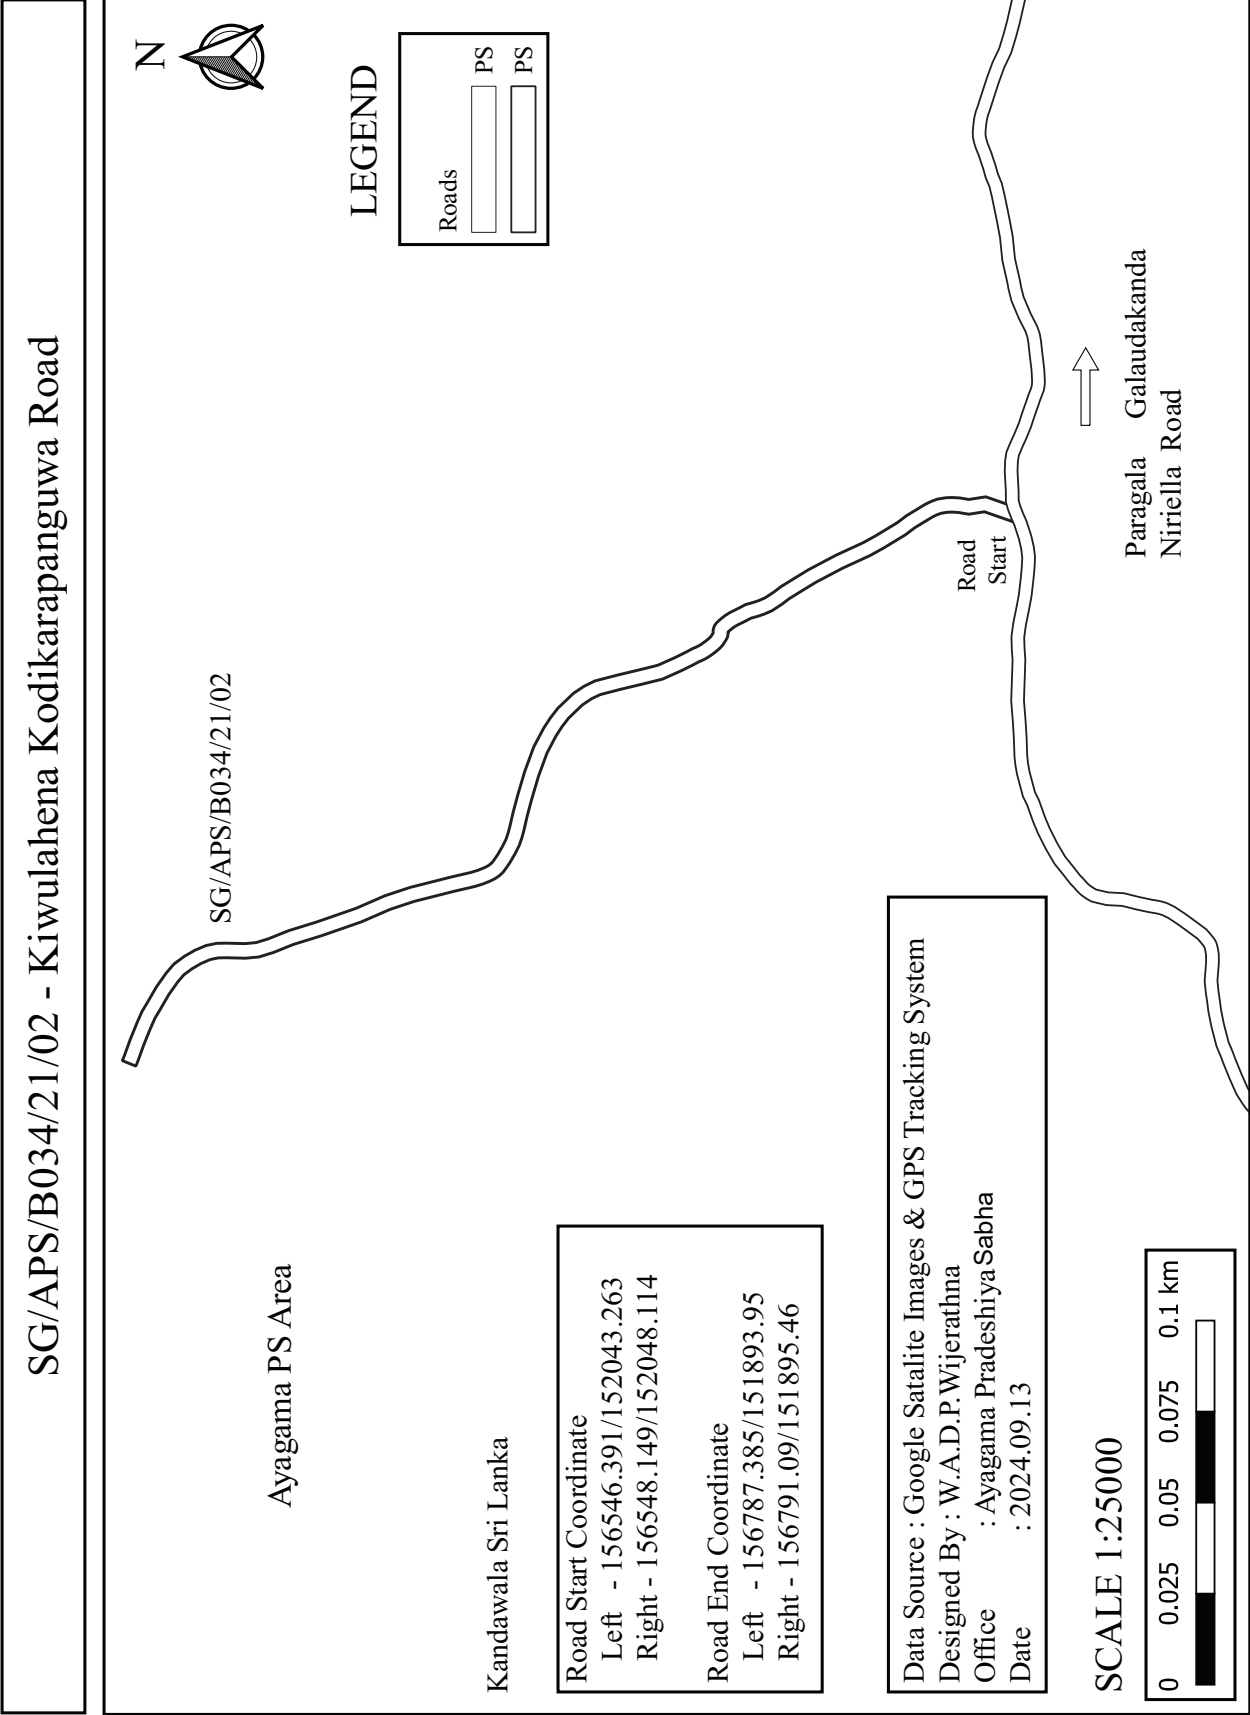



SG/APS/B034/21/02/01 - First Lane of Kiwulahena Kodikarapanguwa Road

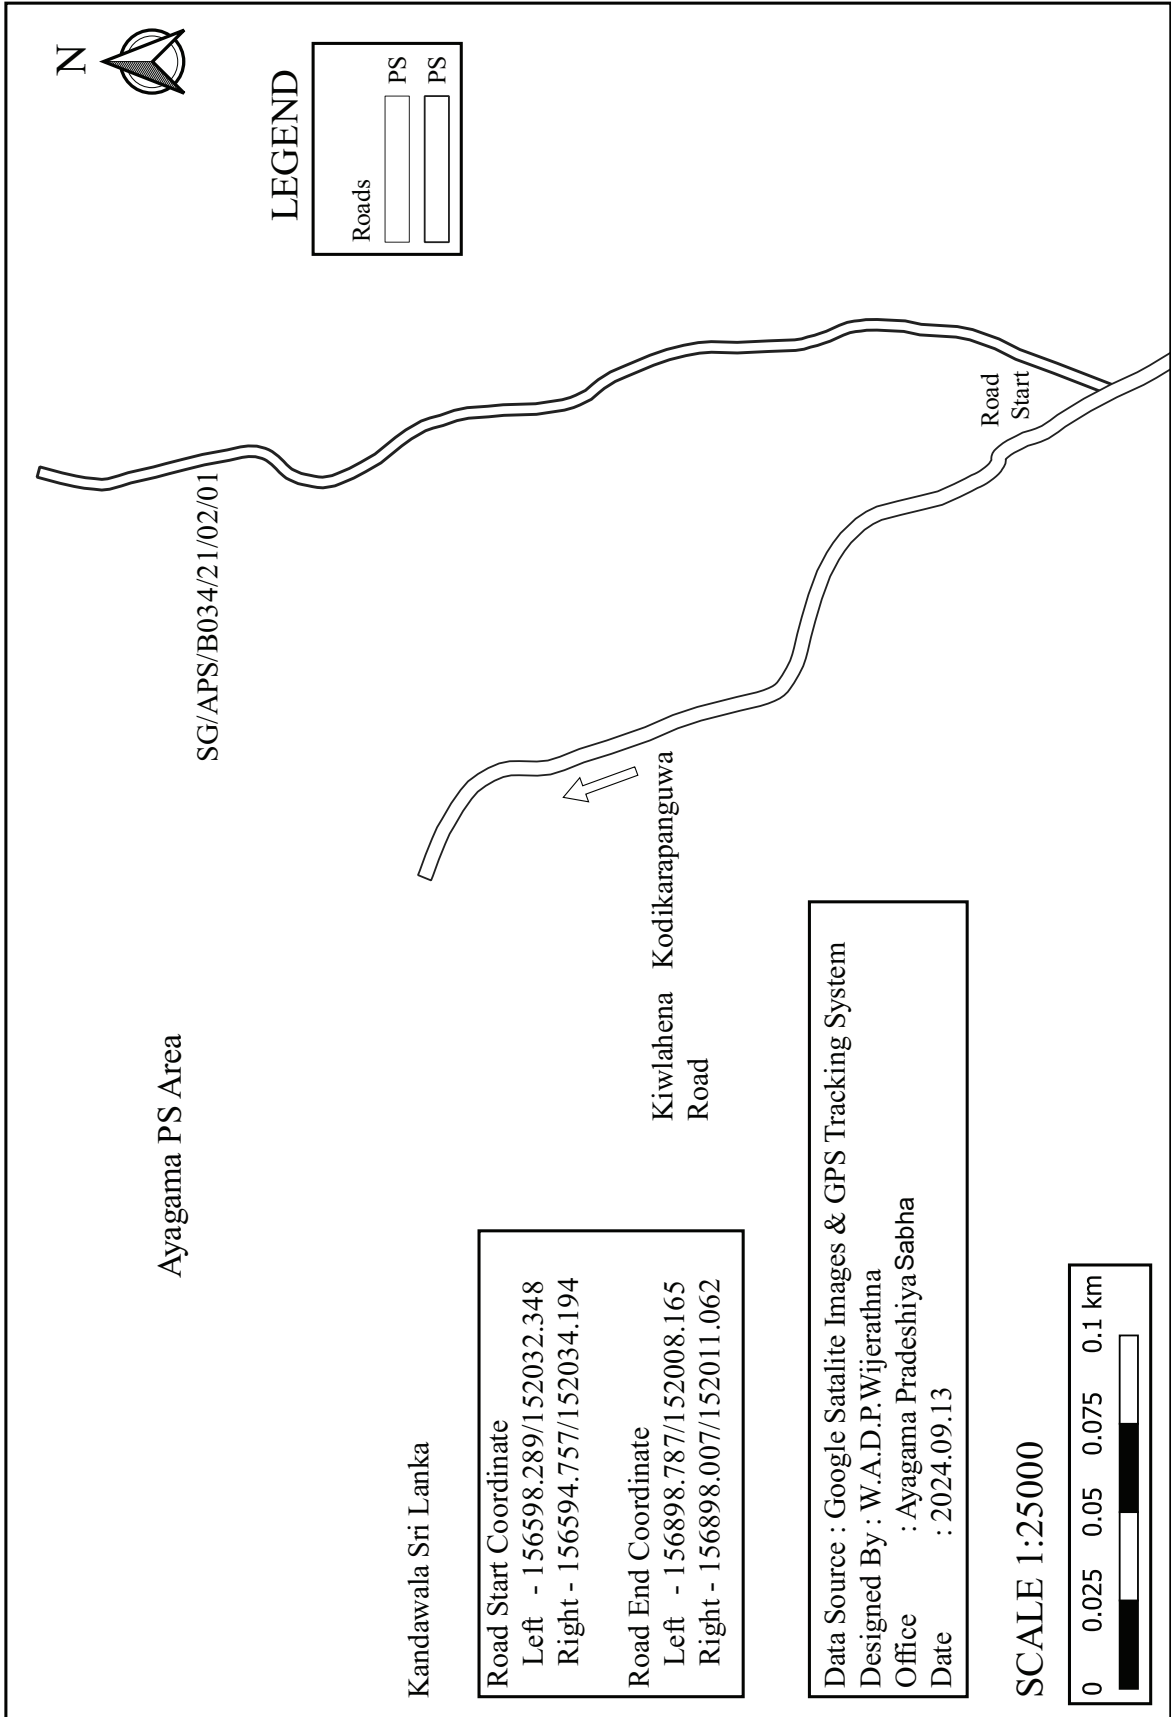


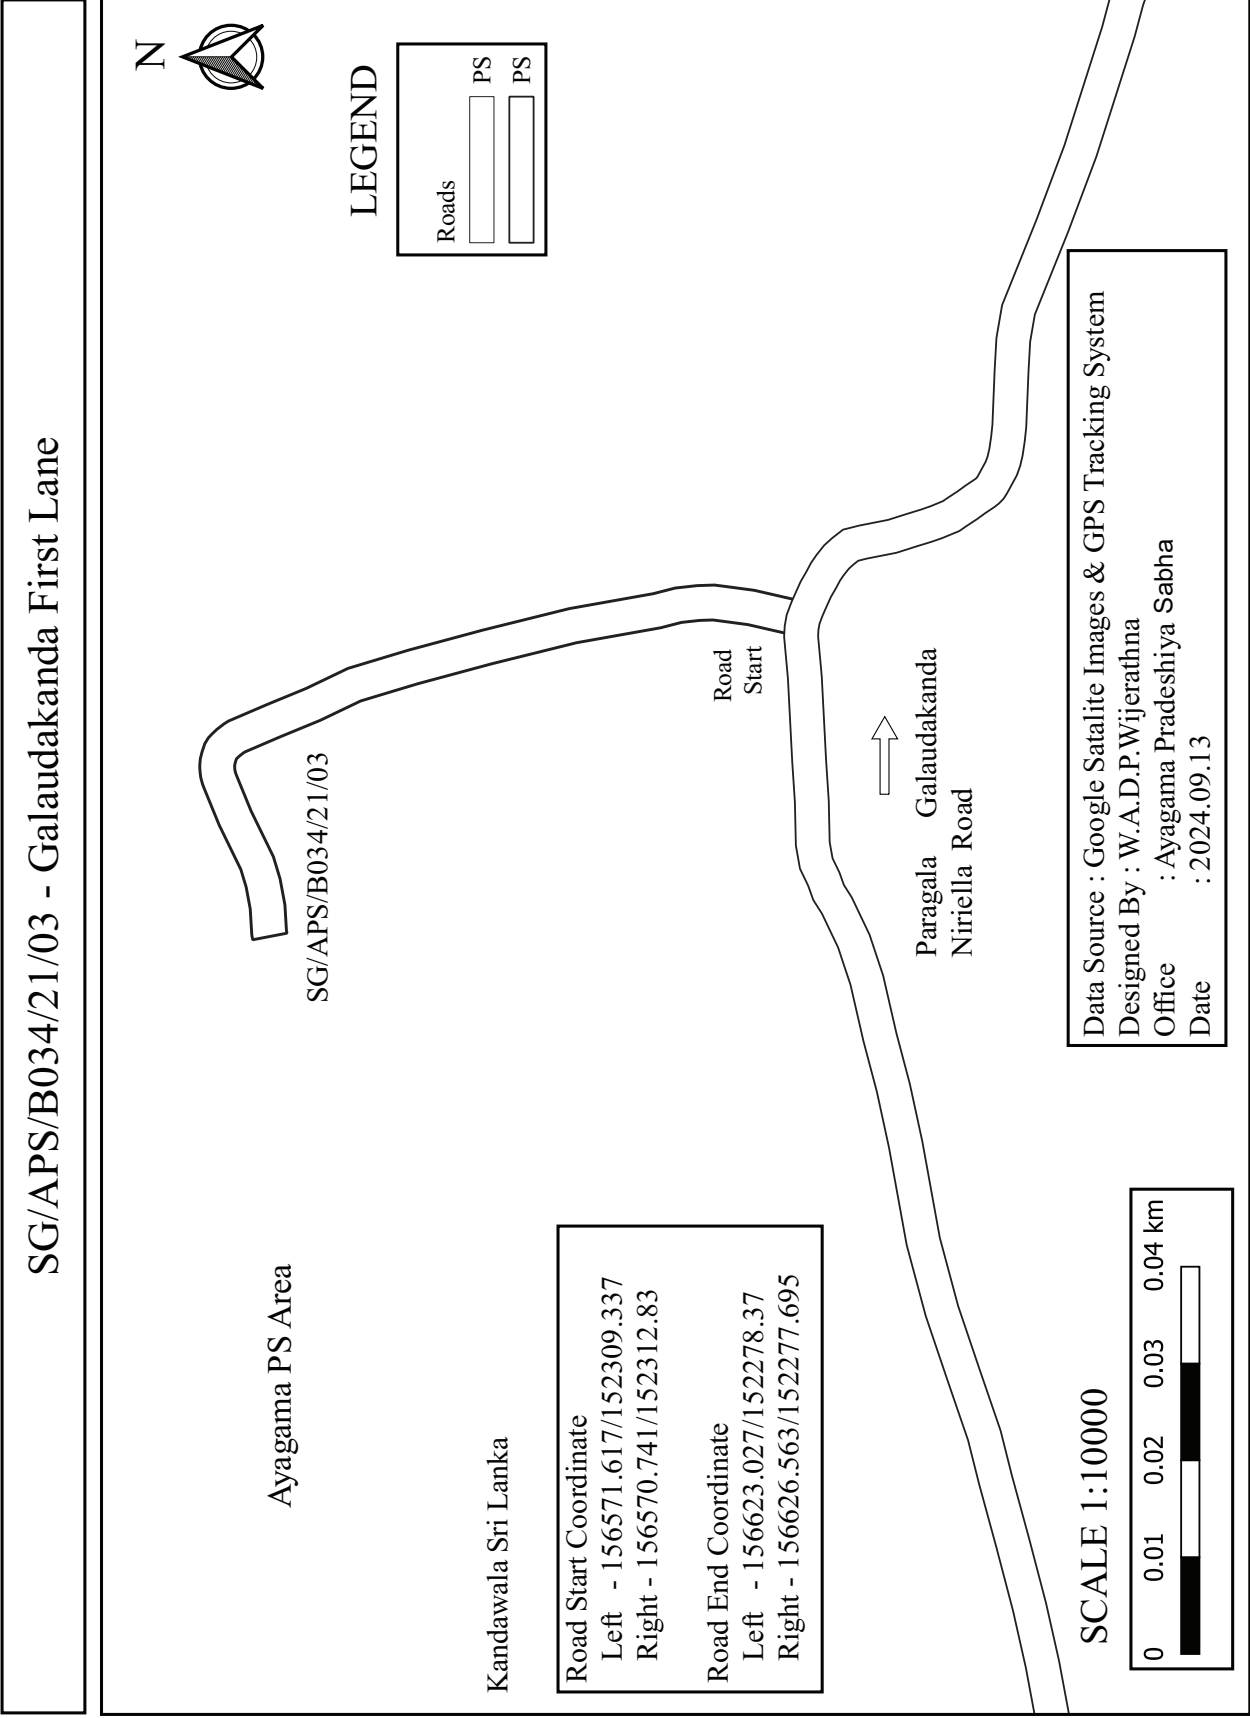


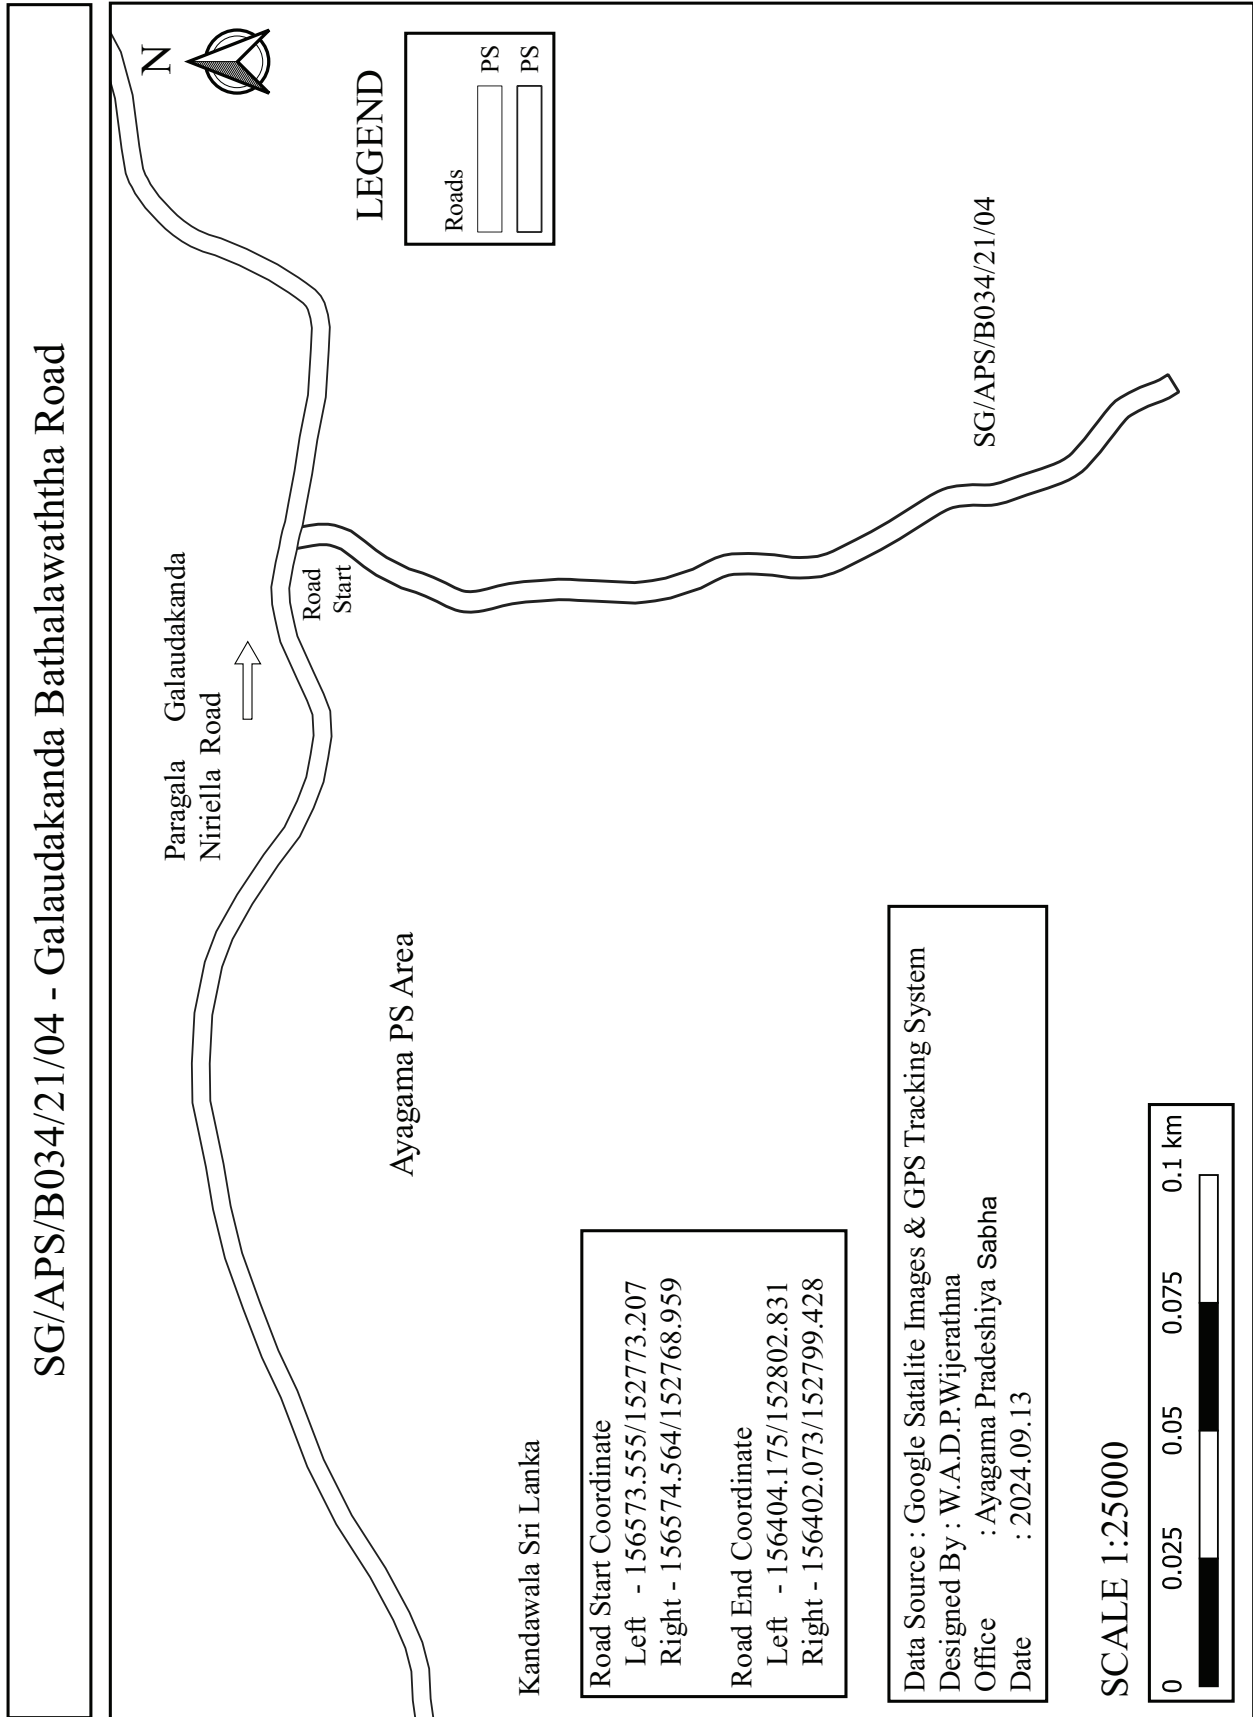


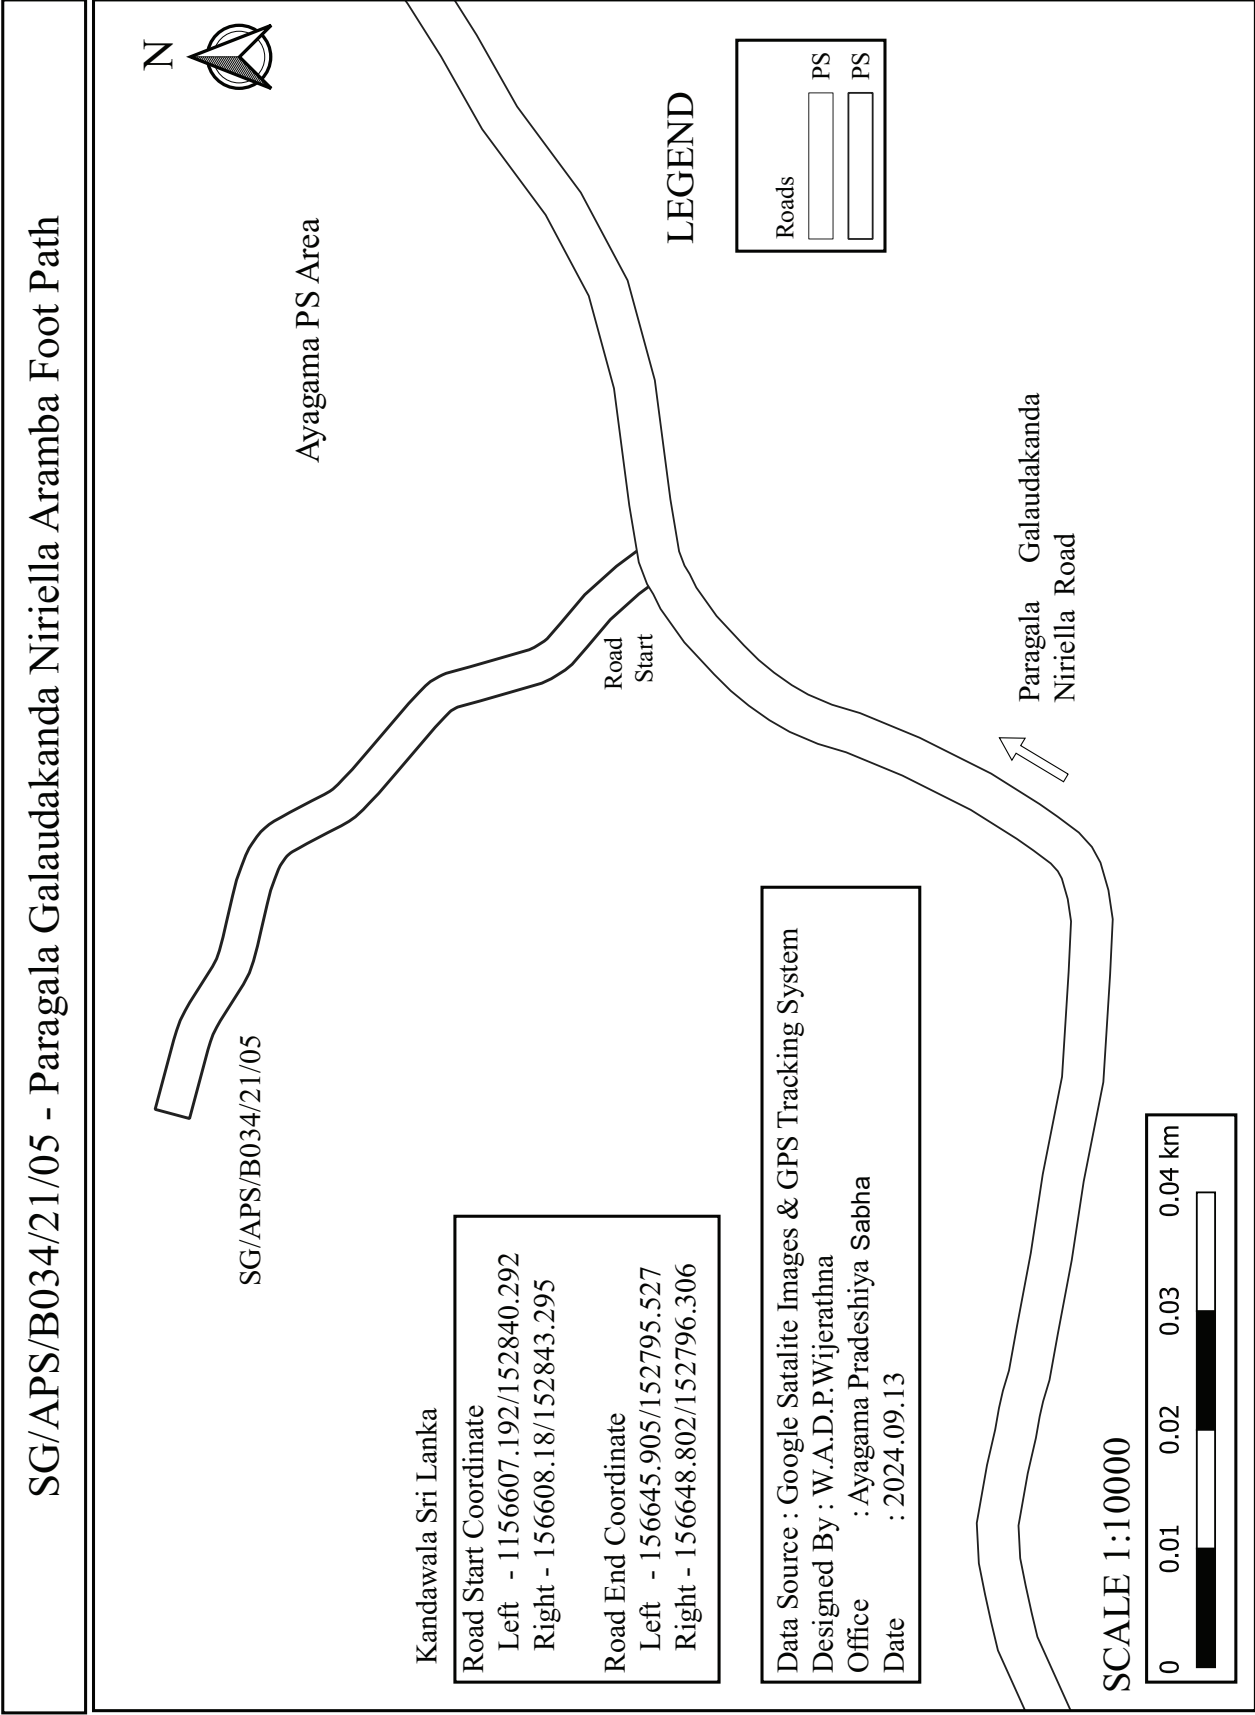


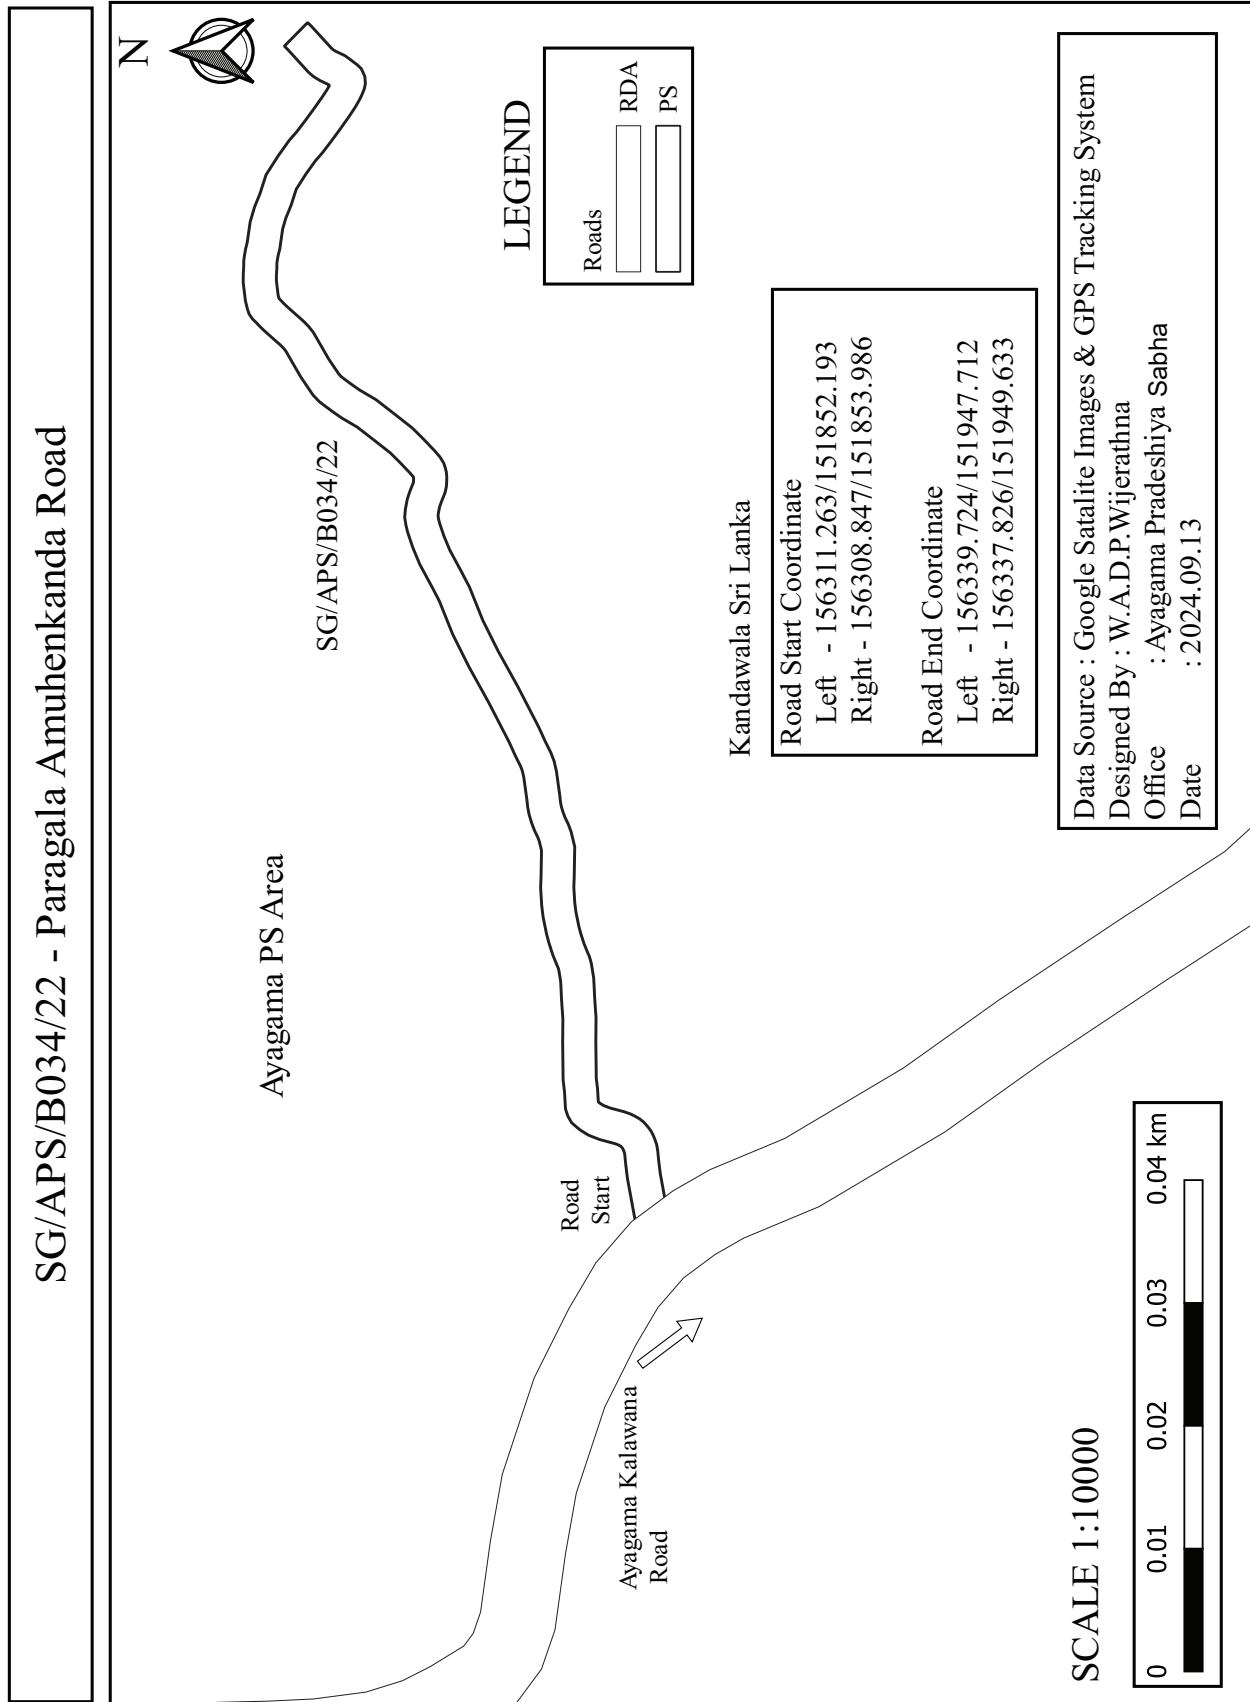


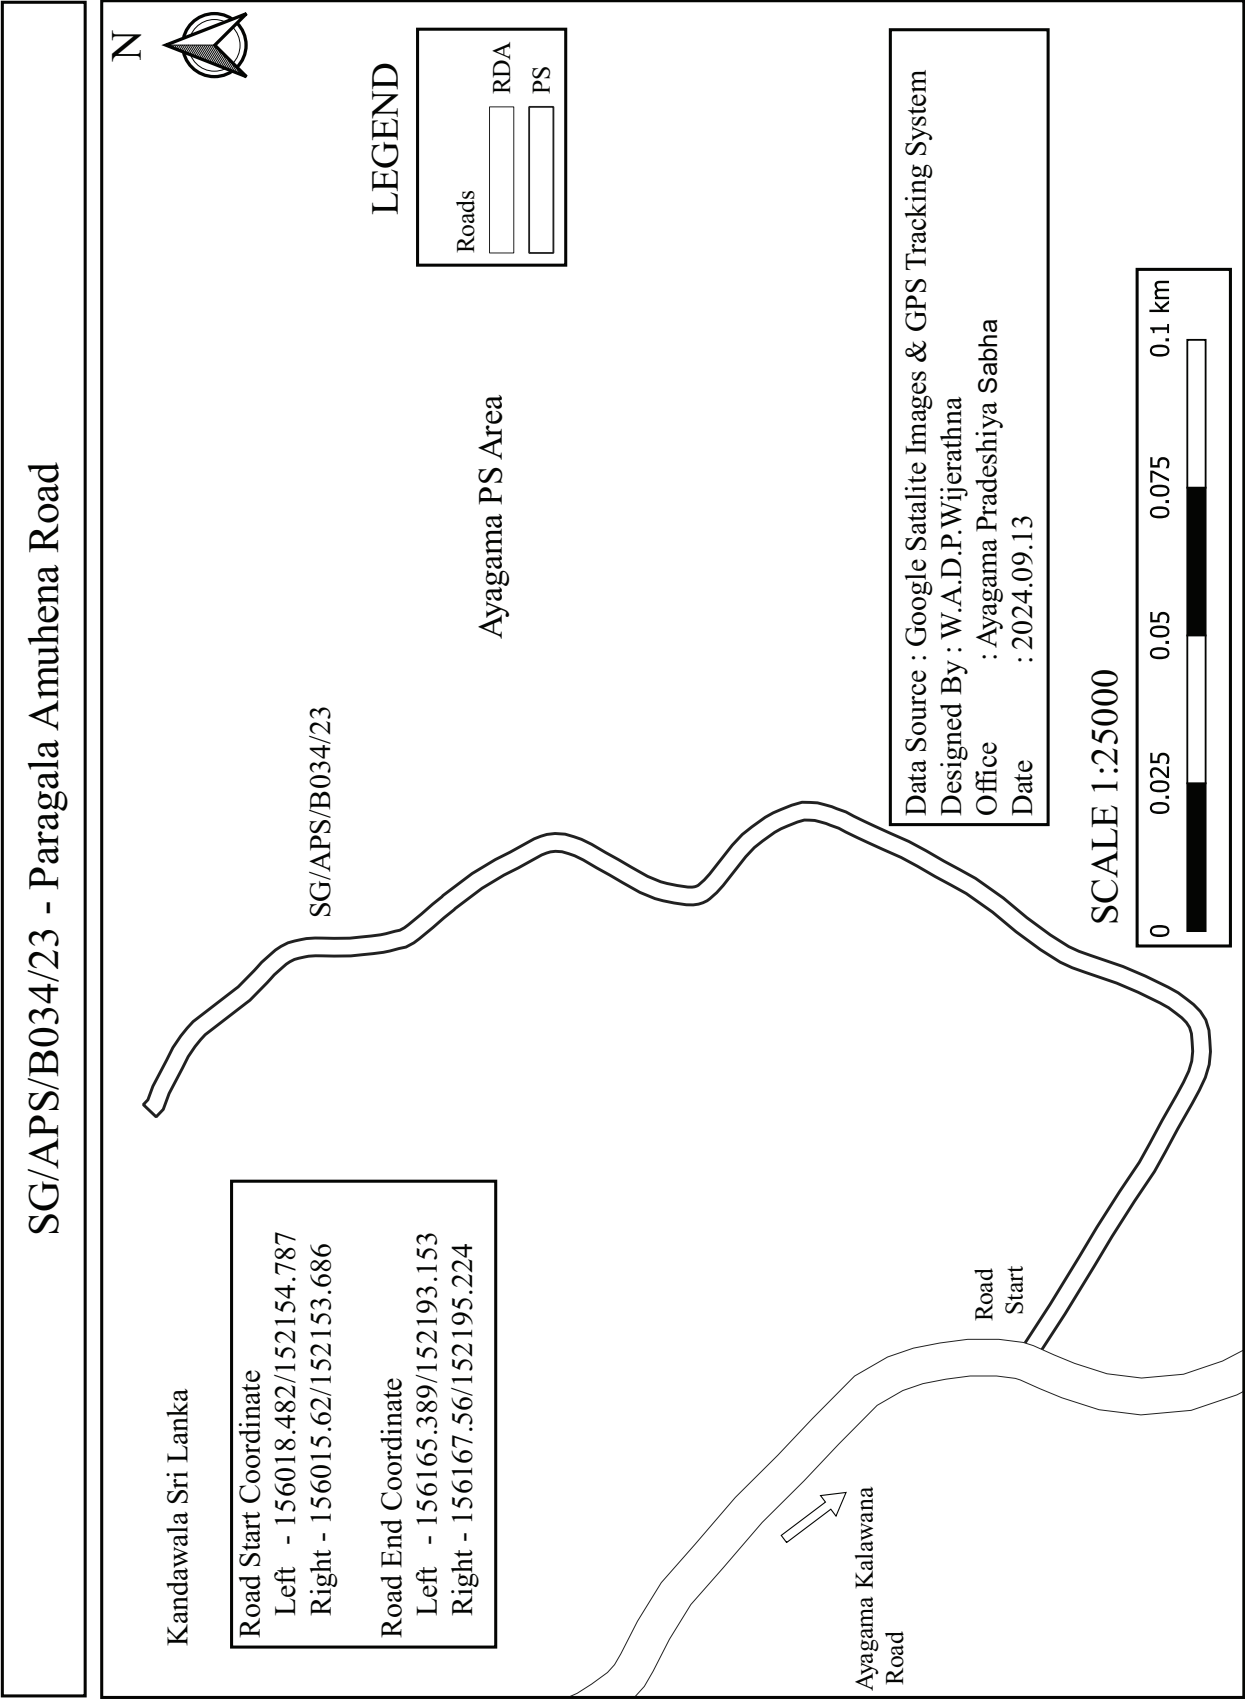

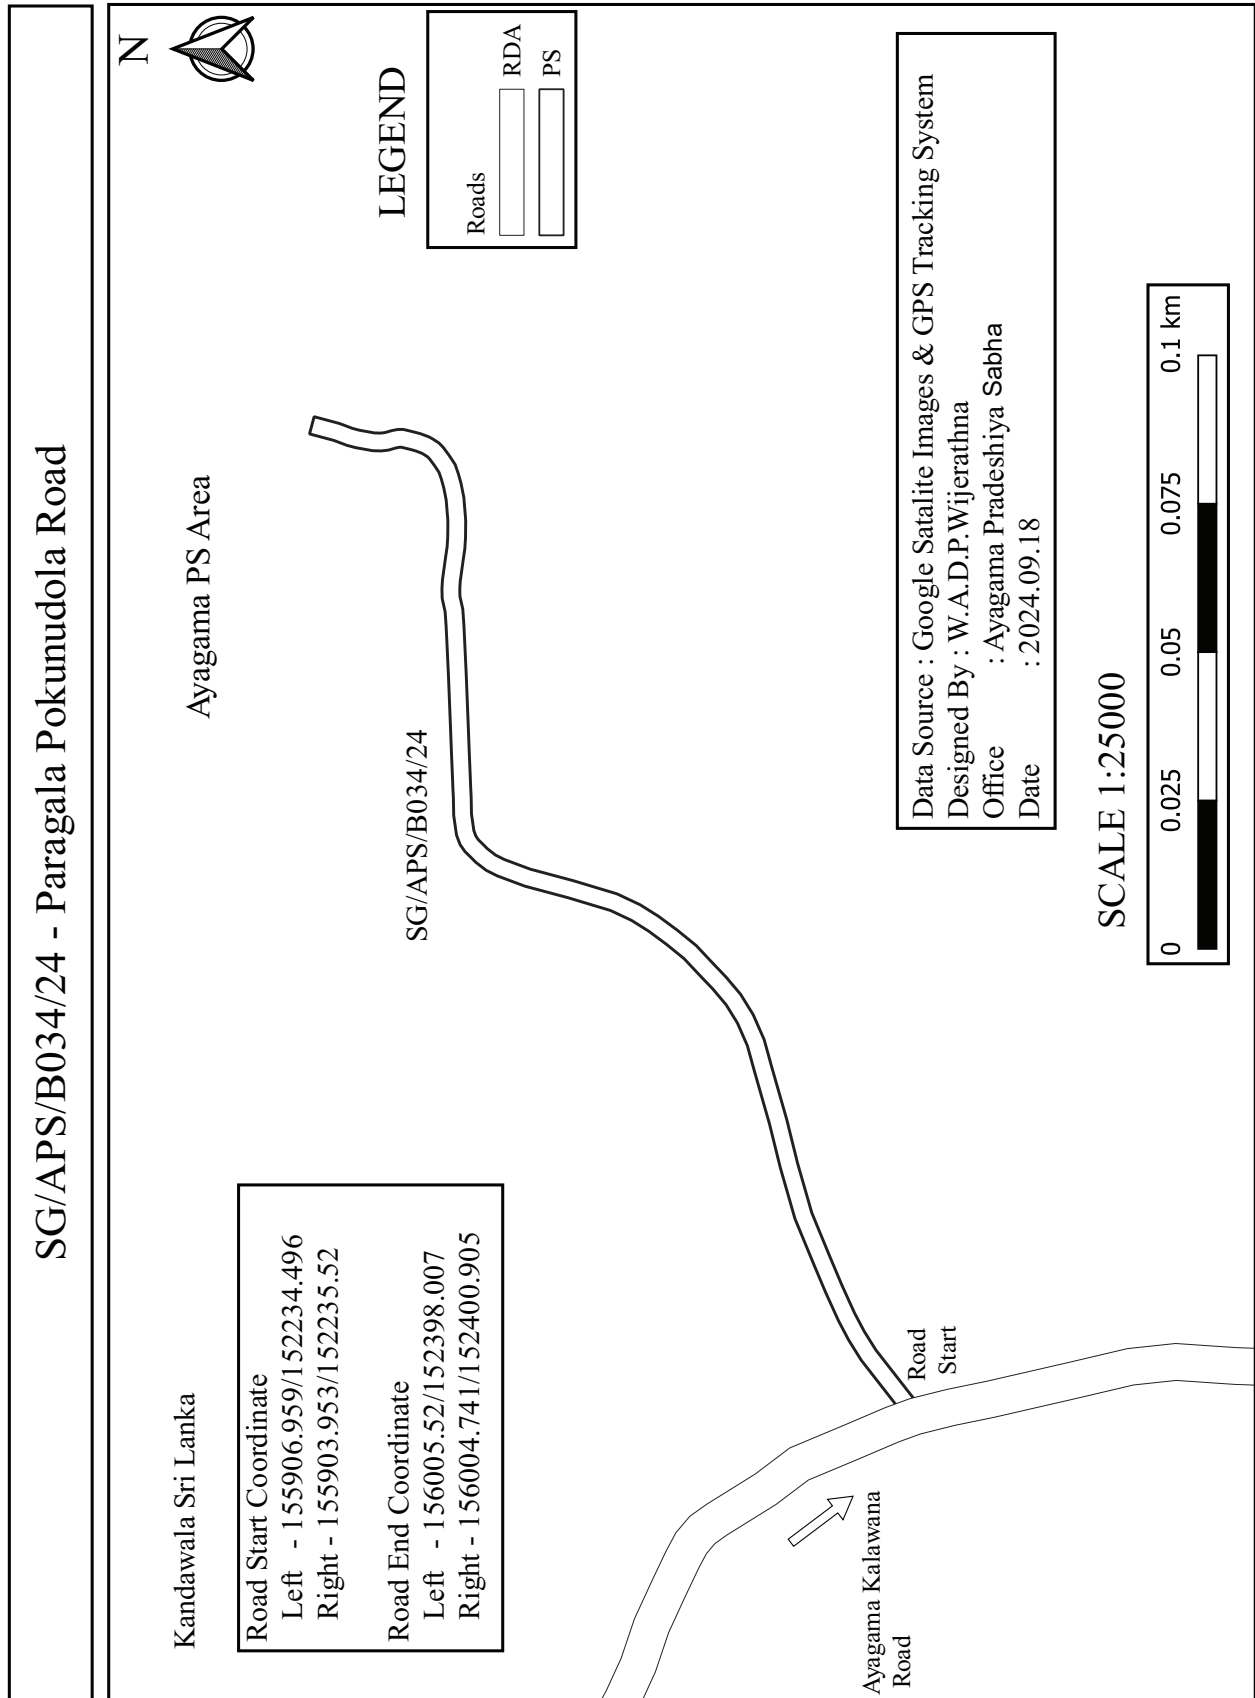


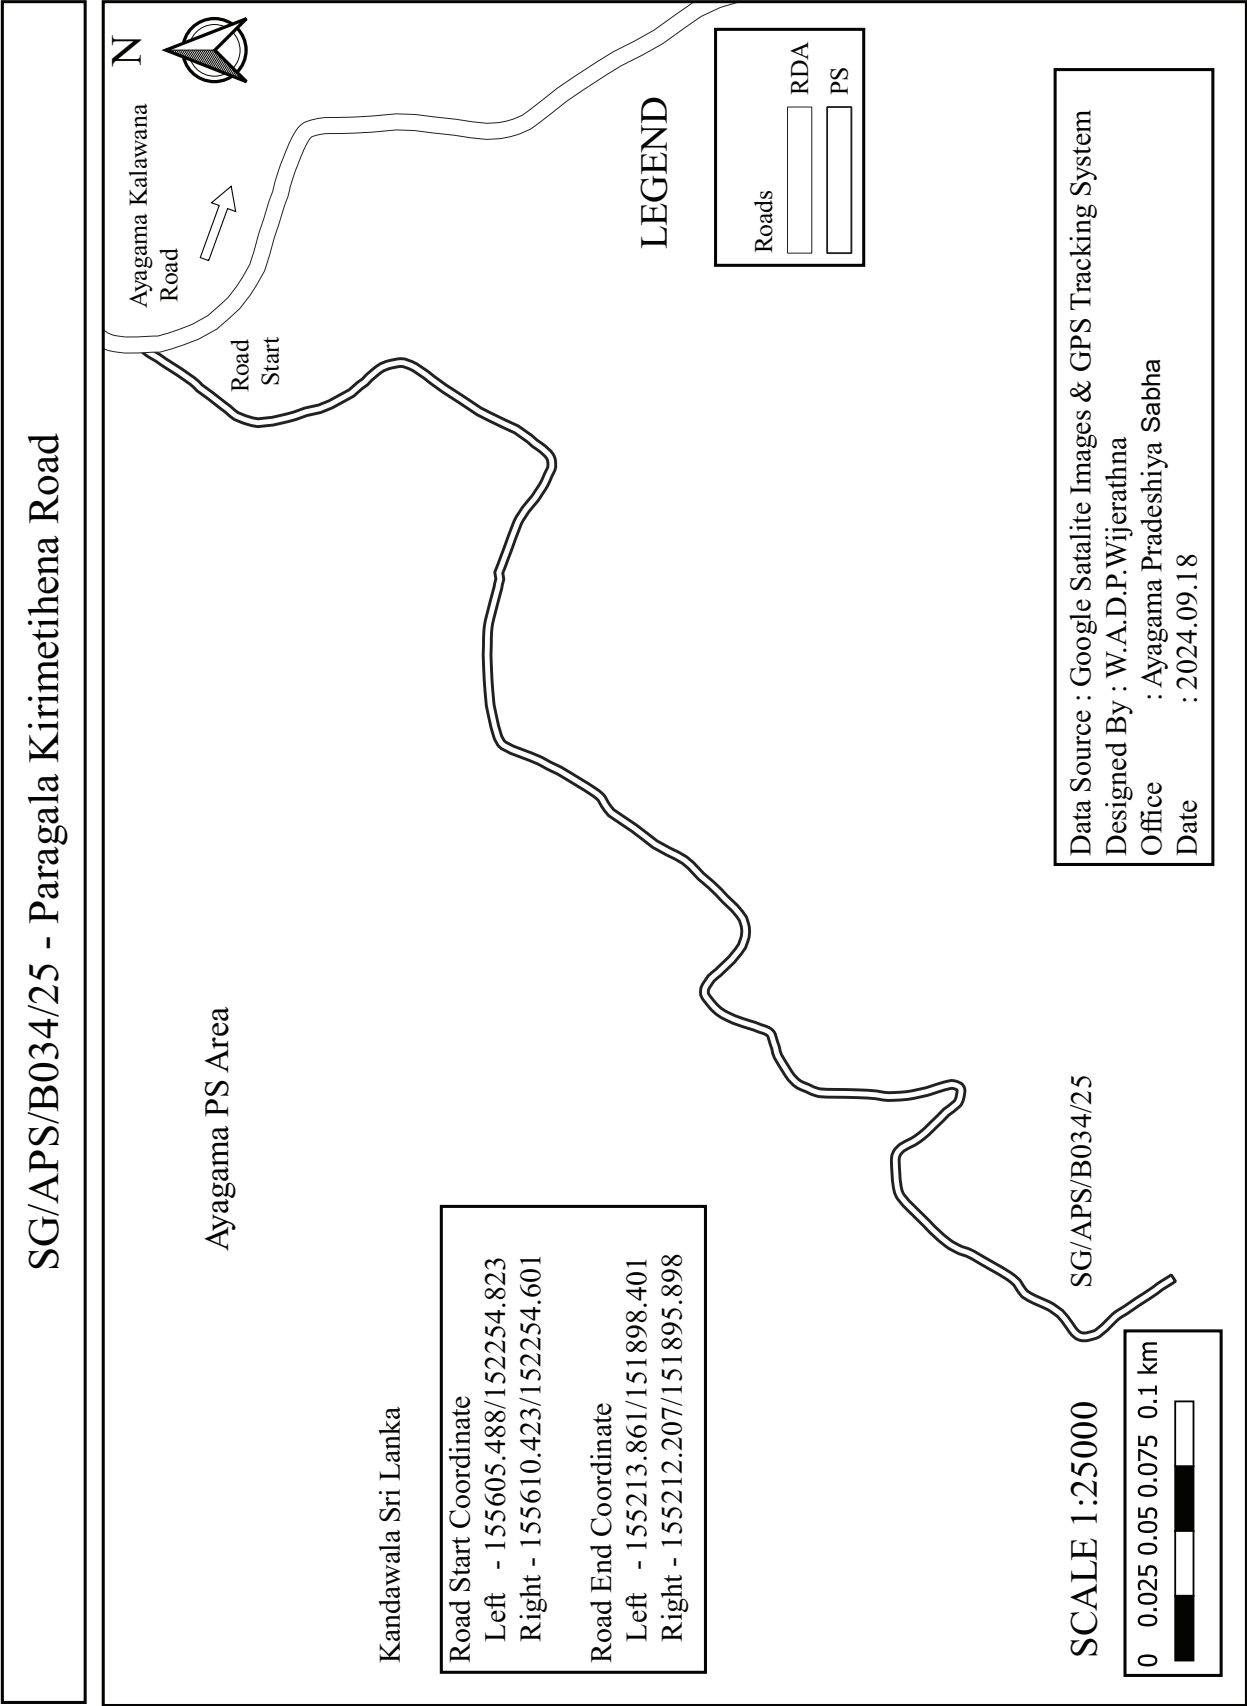


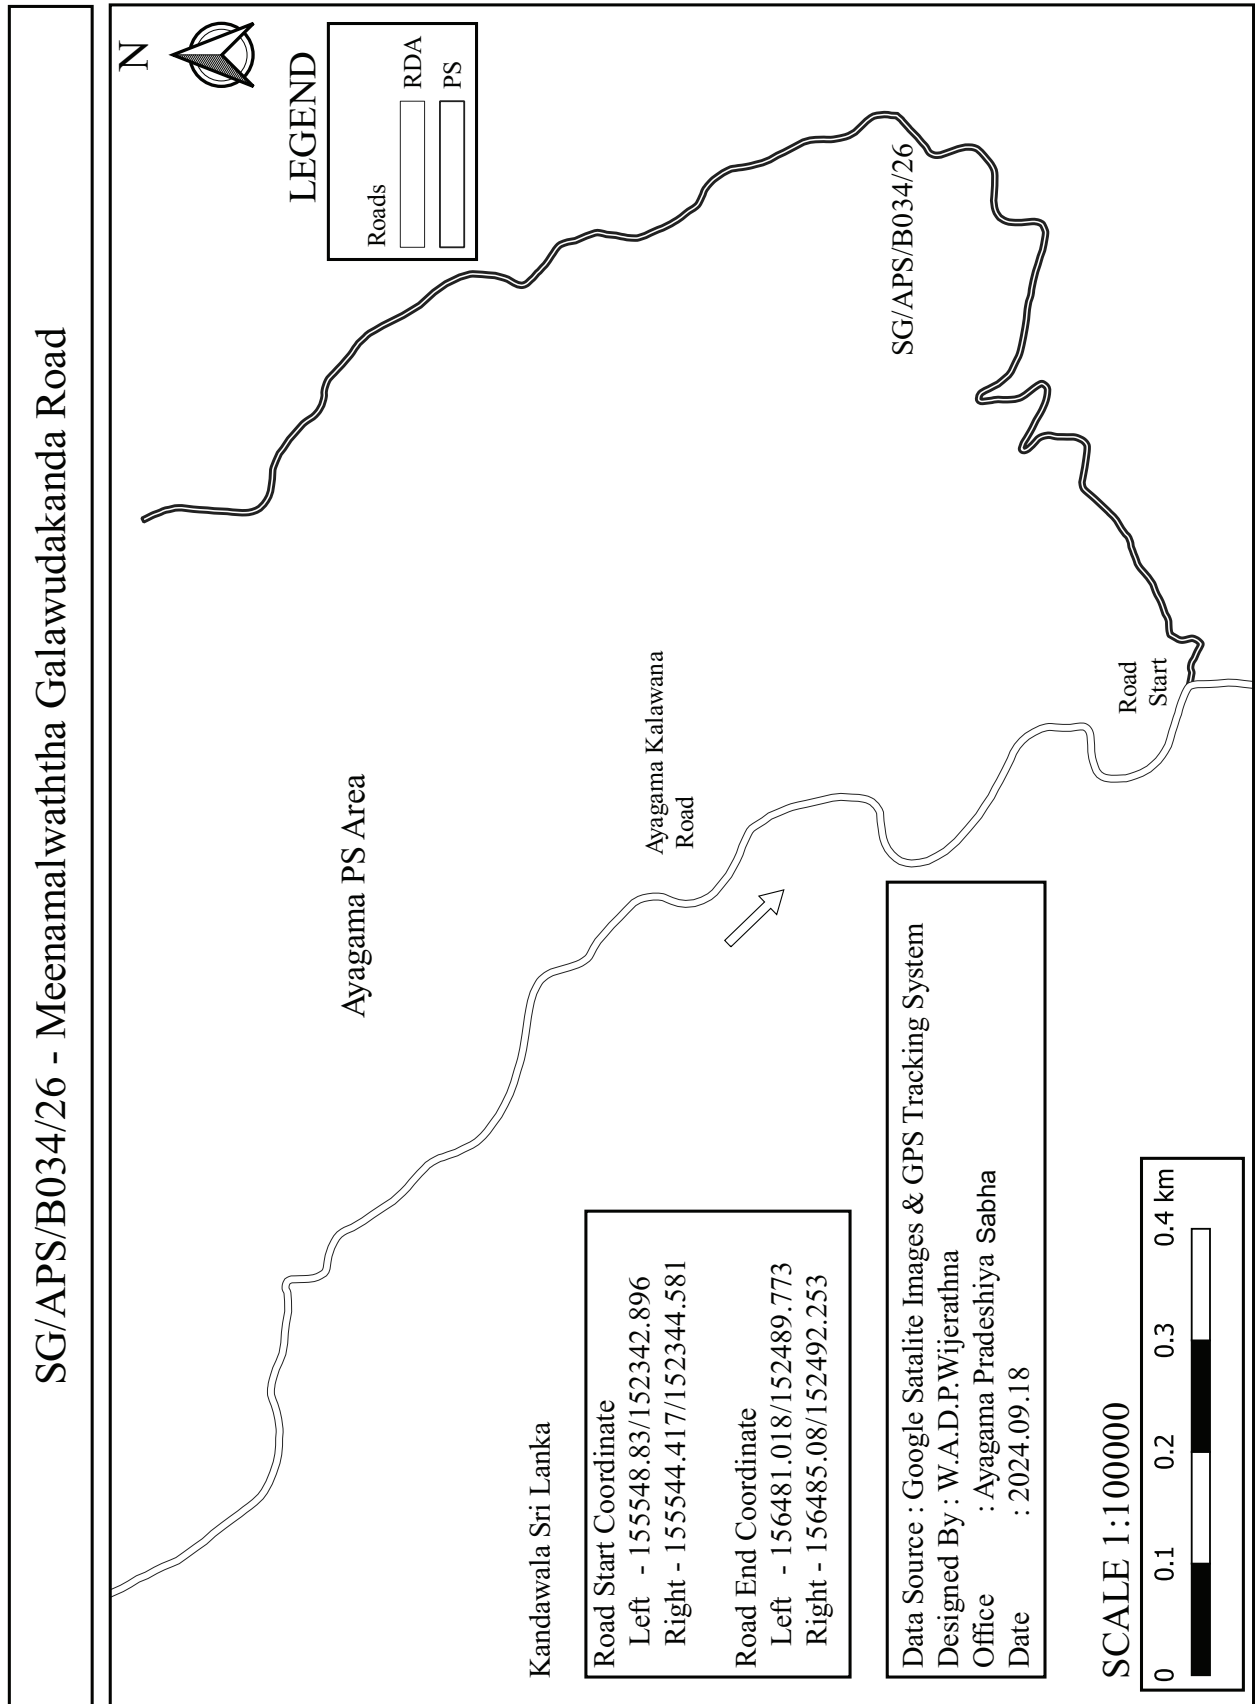


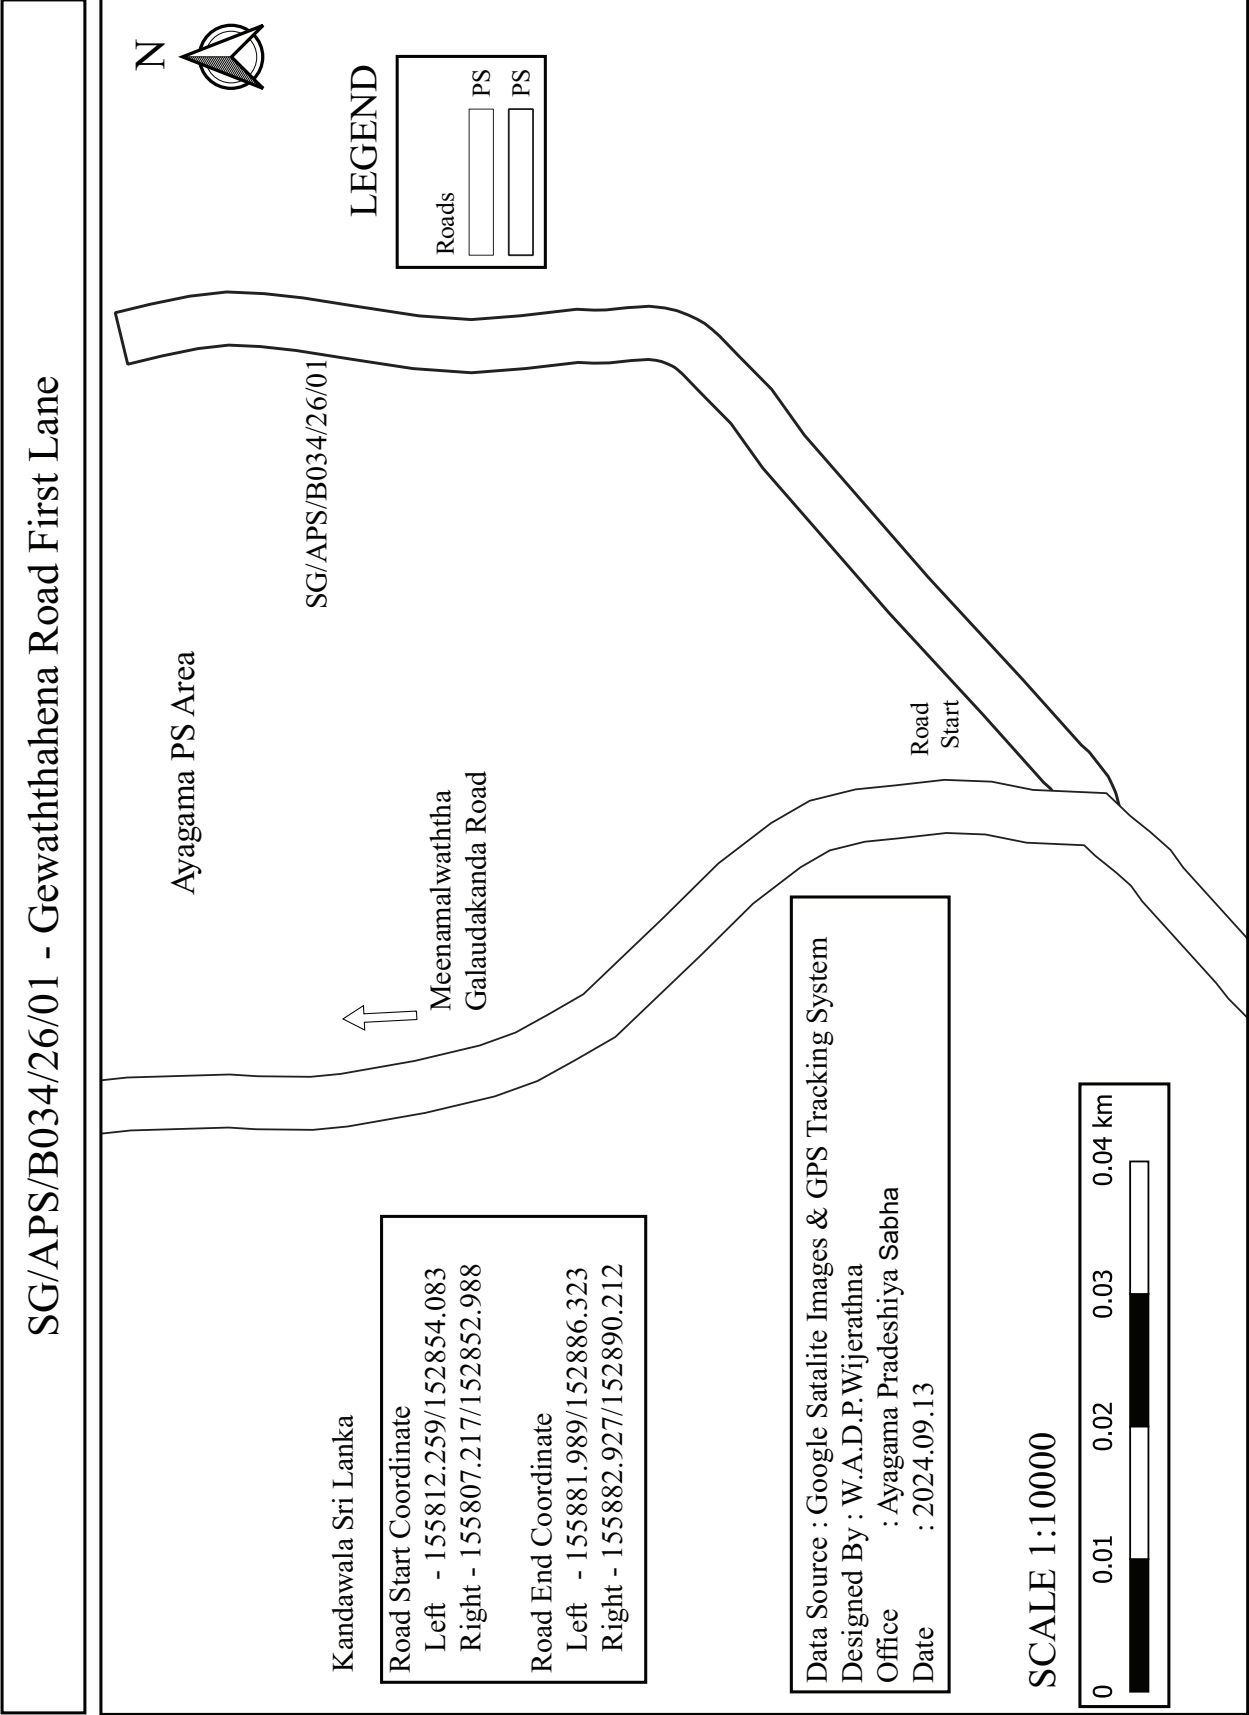



SG/APS/B034/26/02 - Gewathathena Road Second Lane

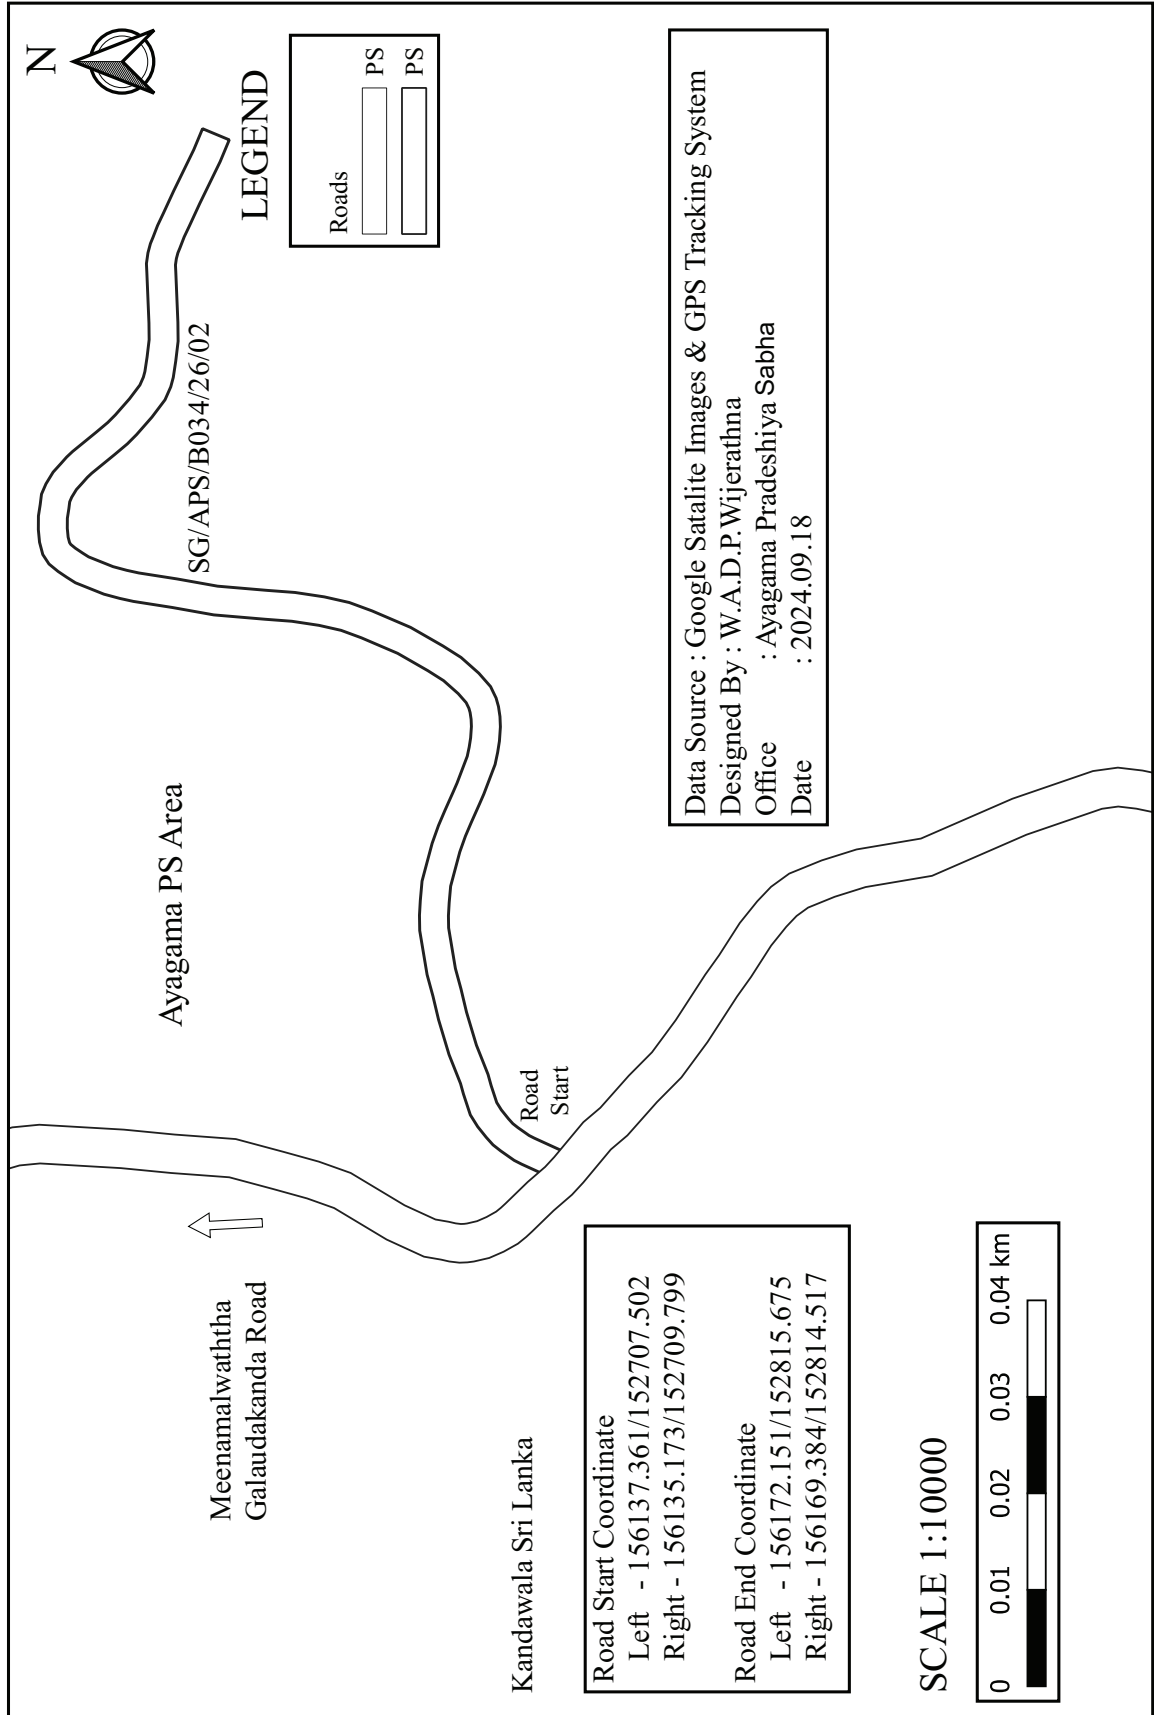


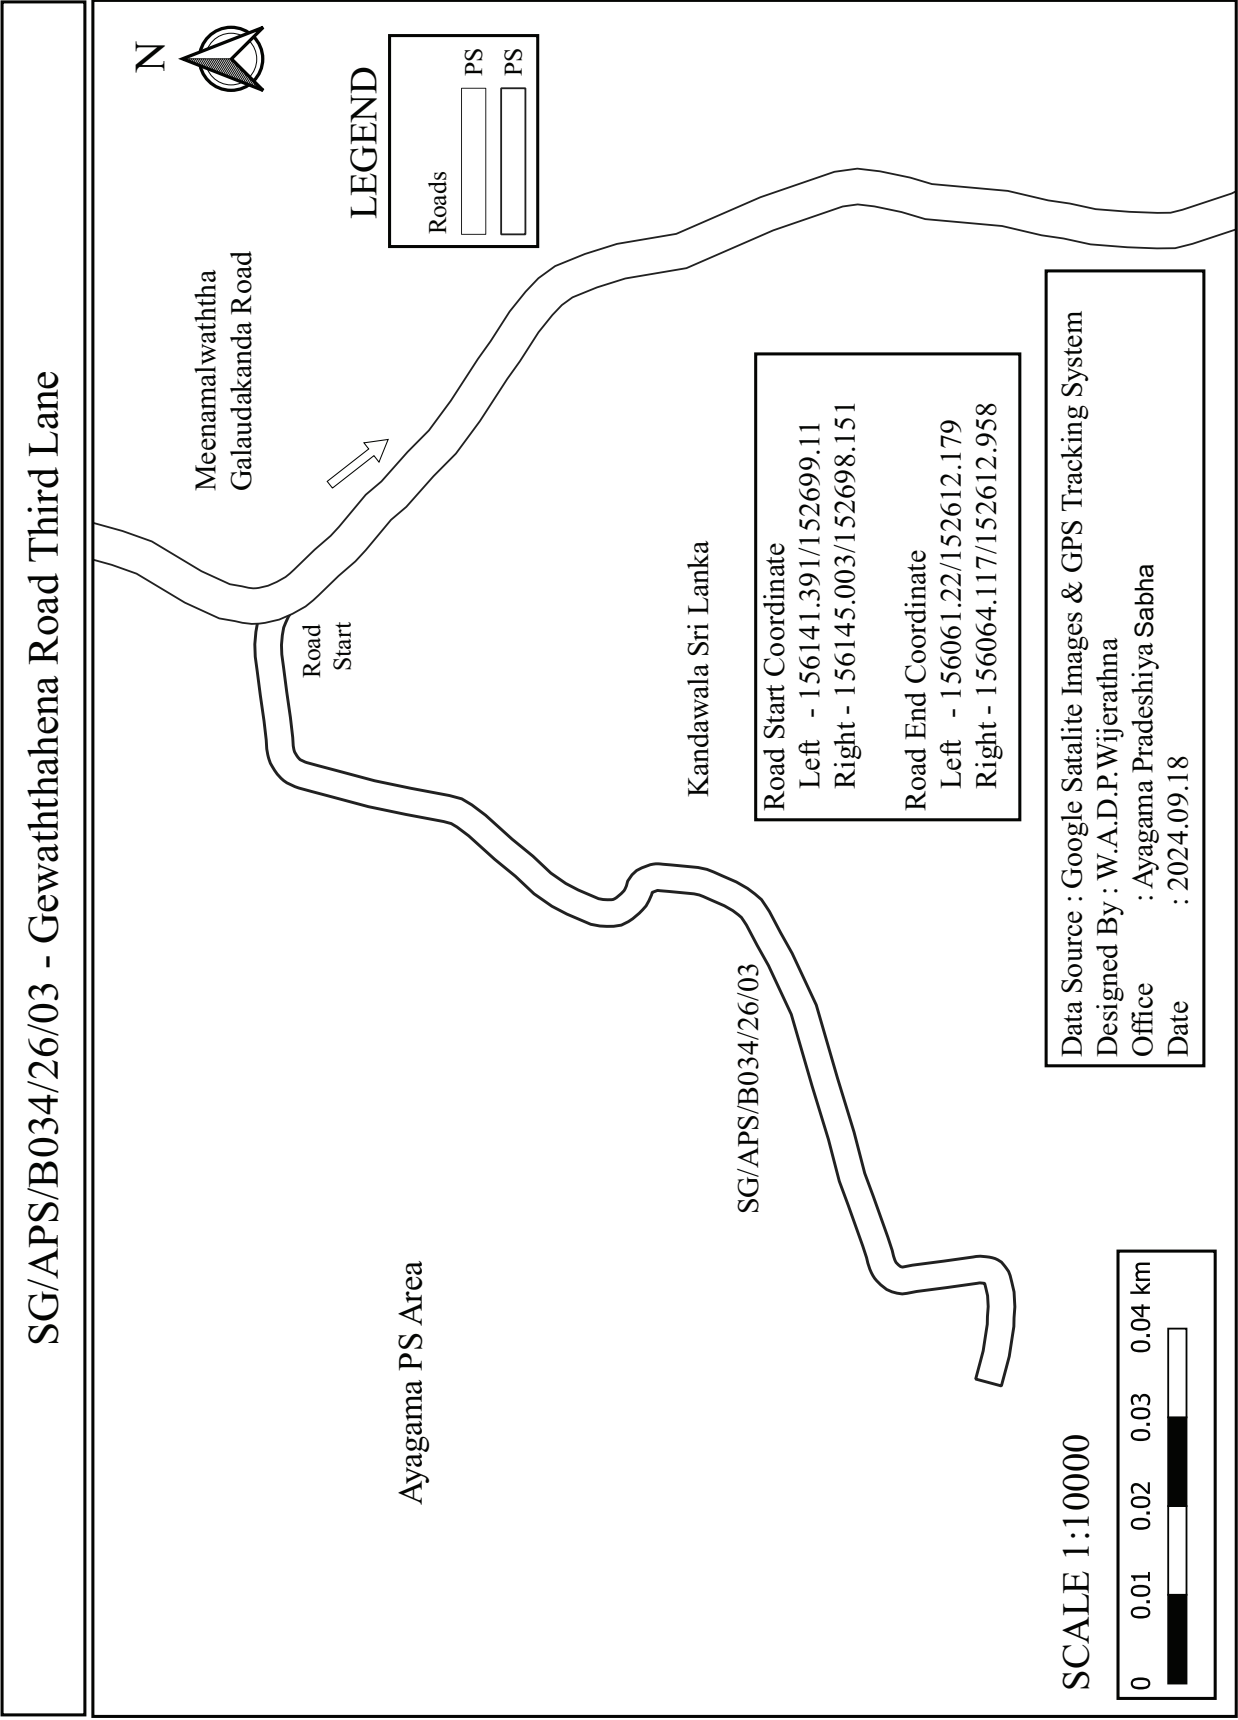


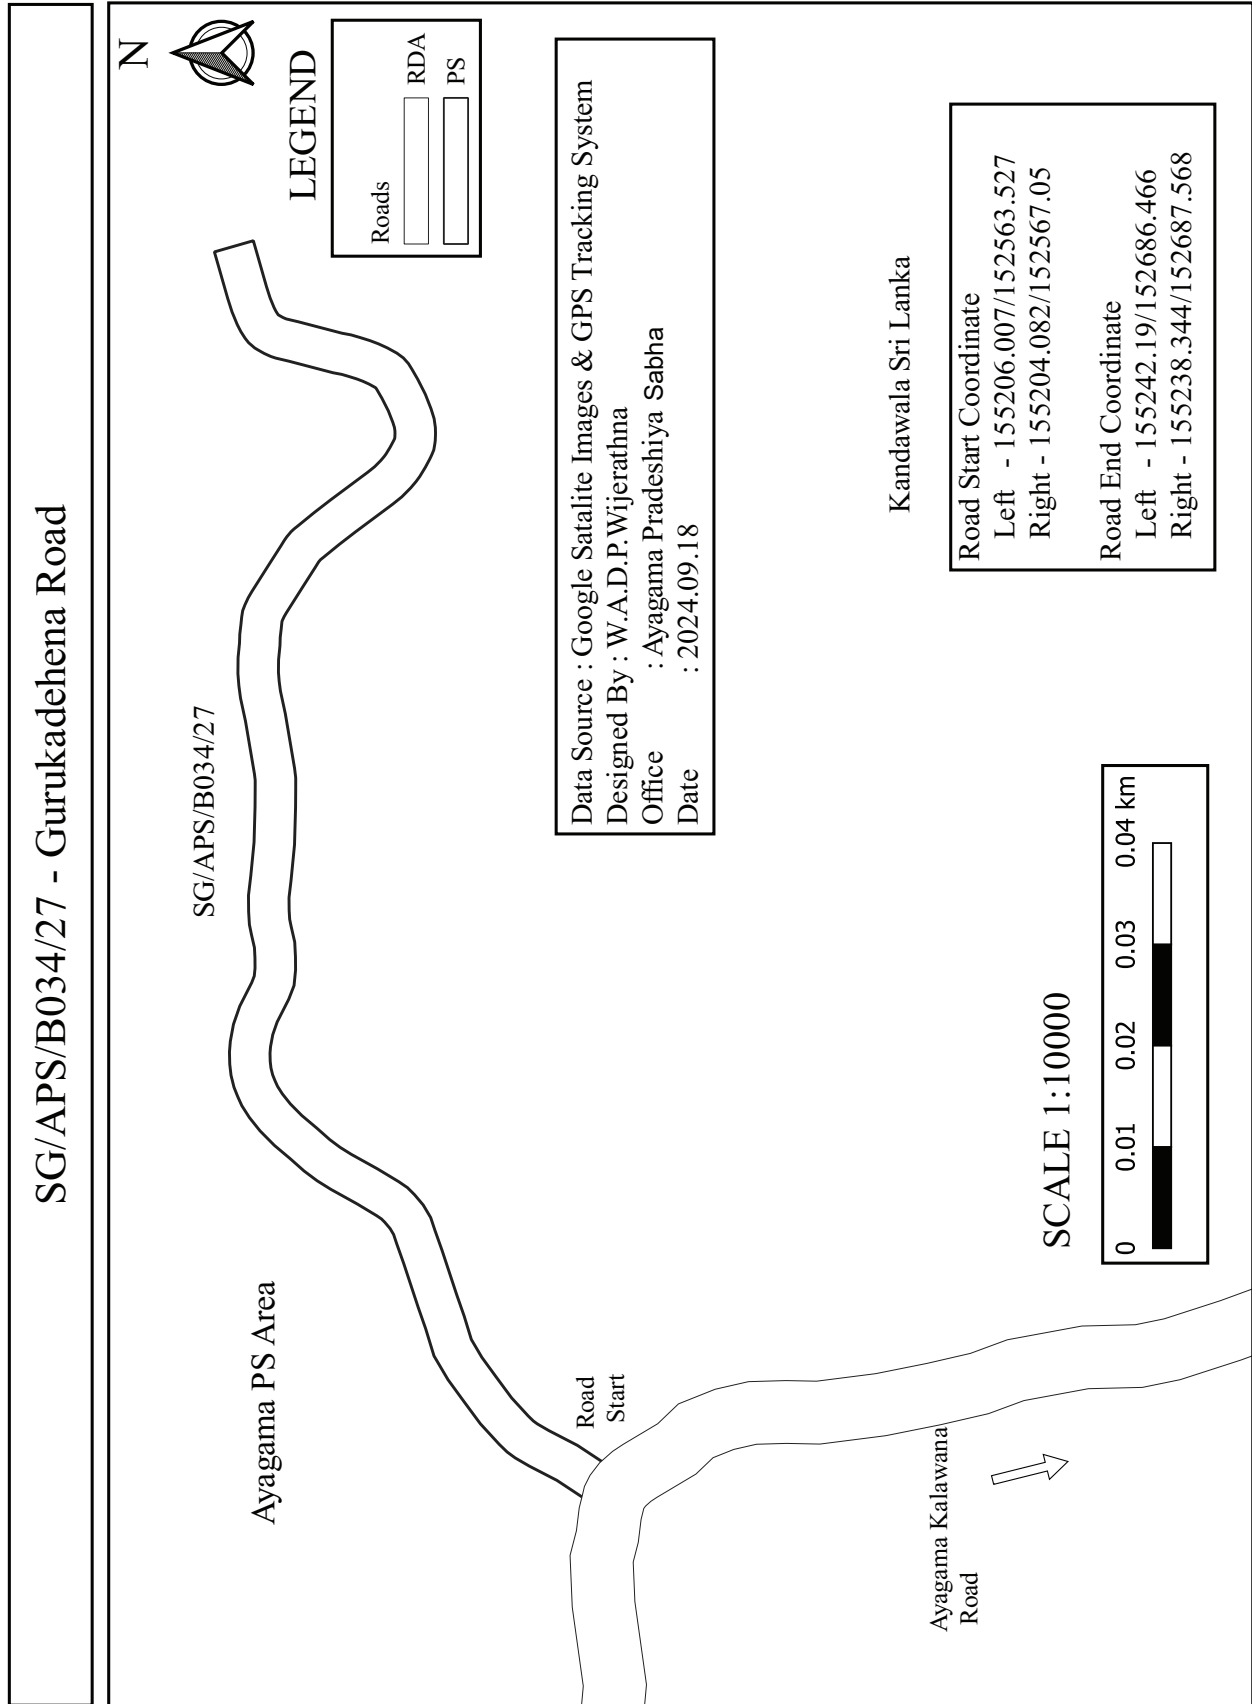


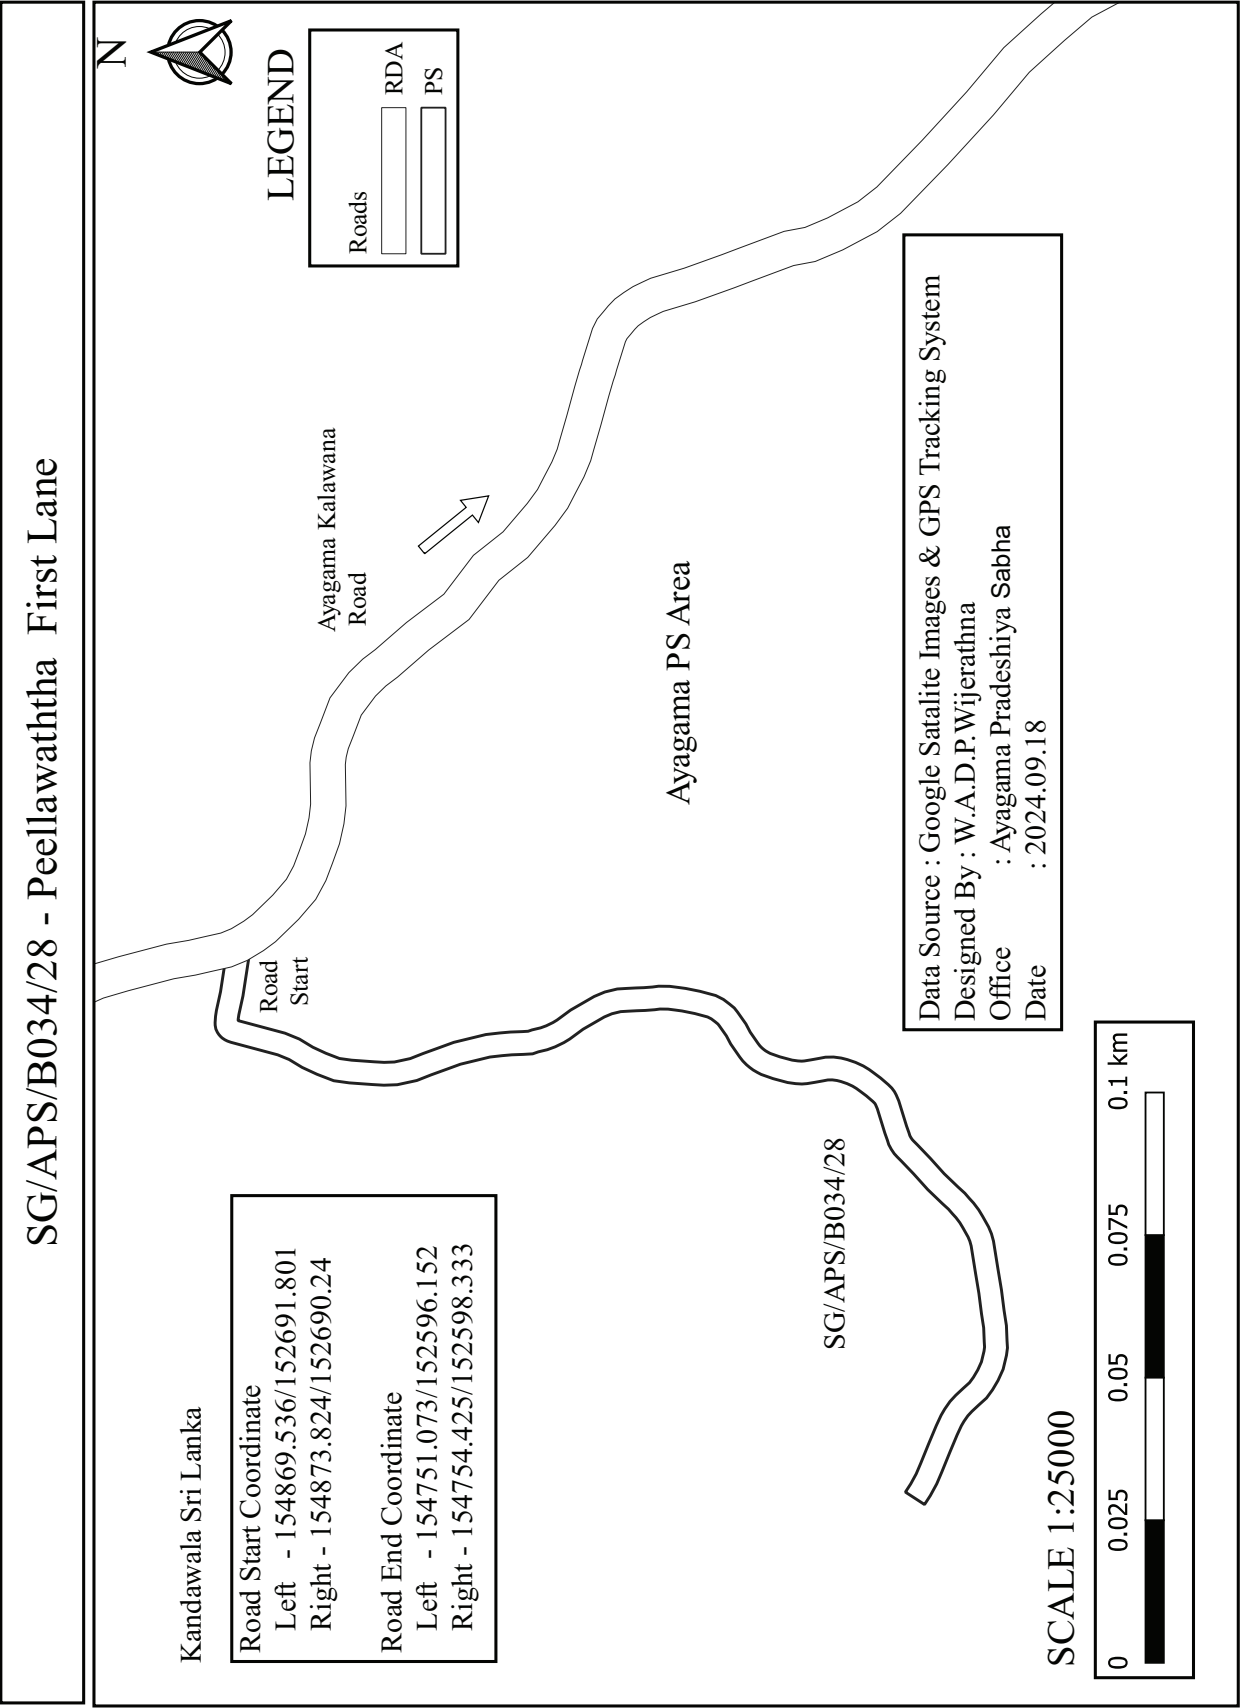

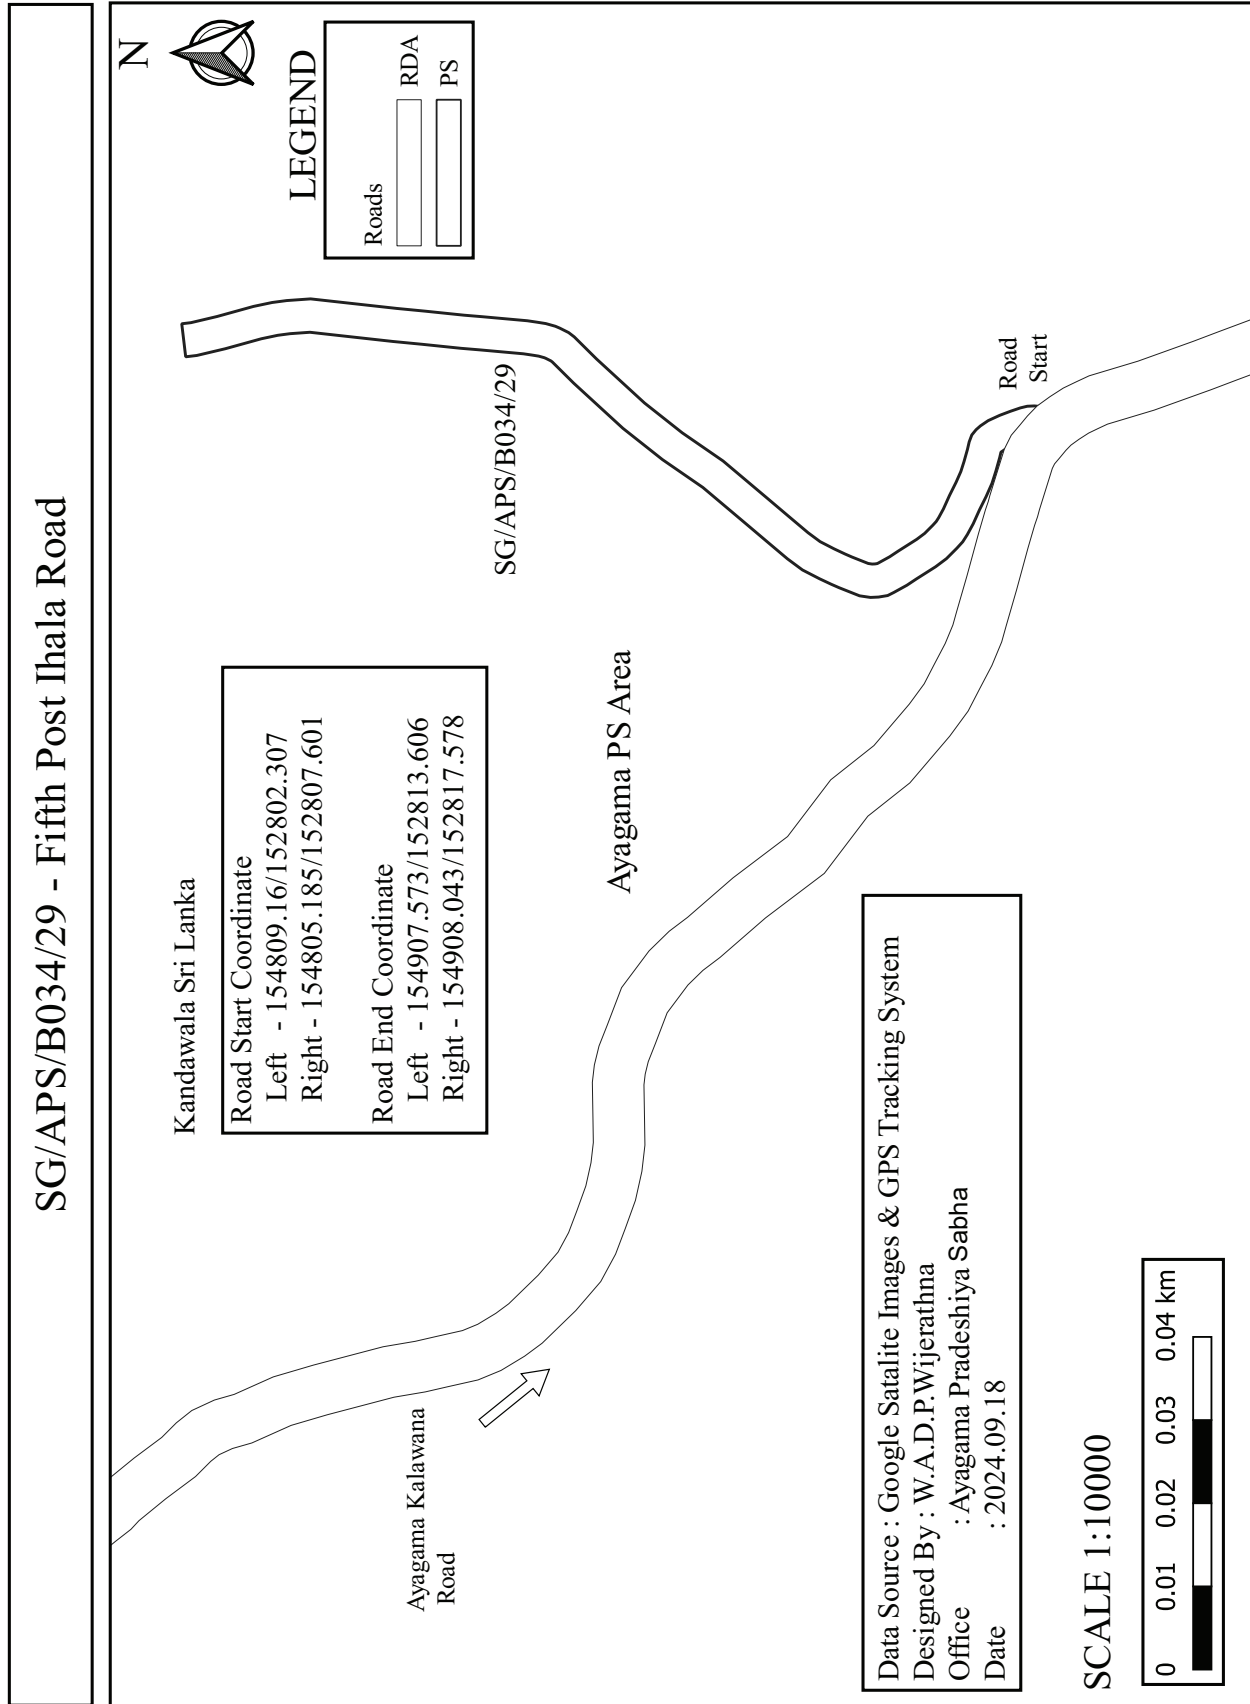


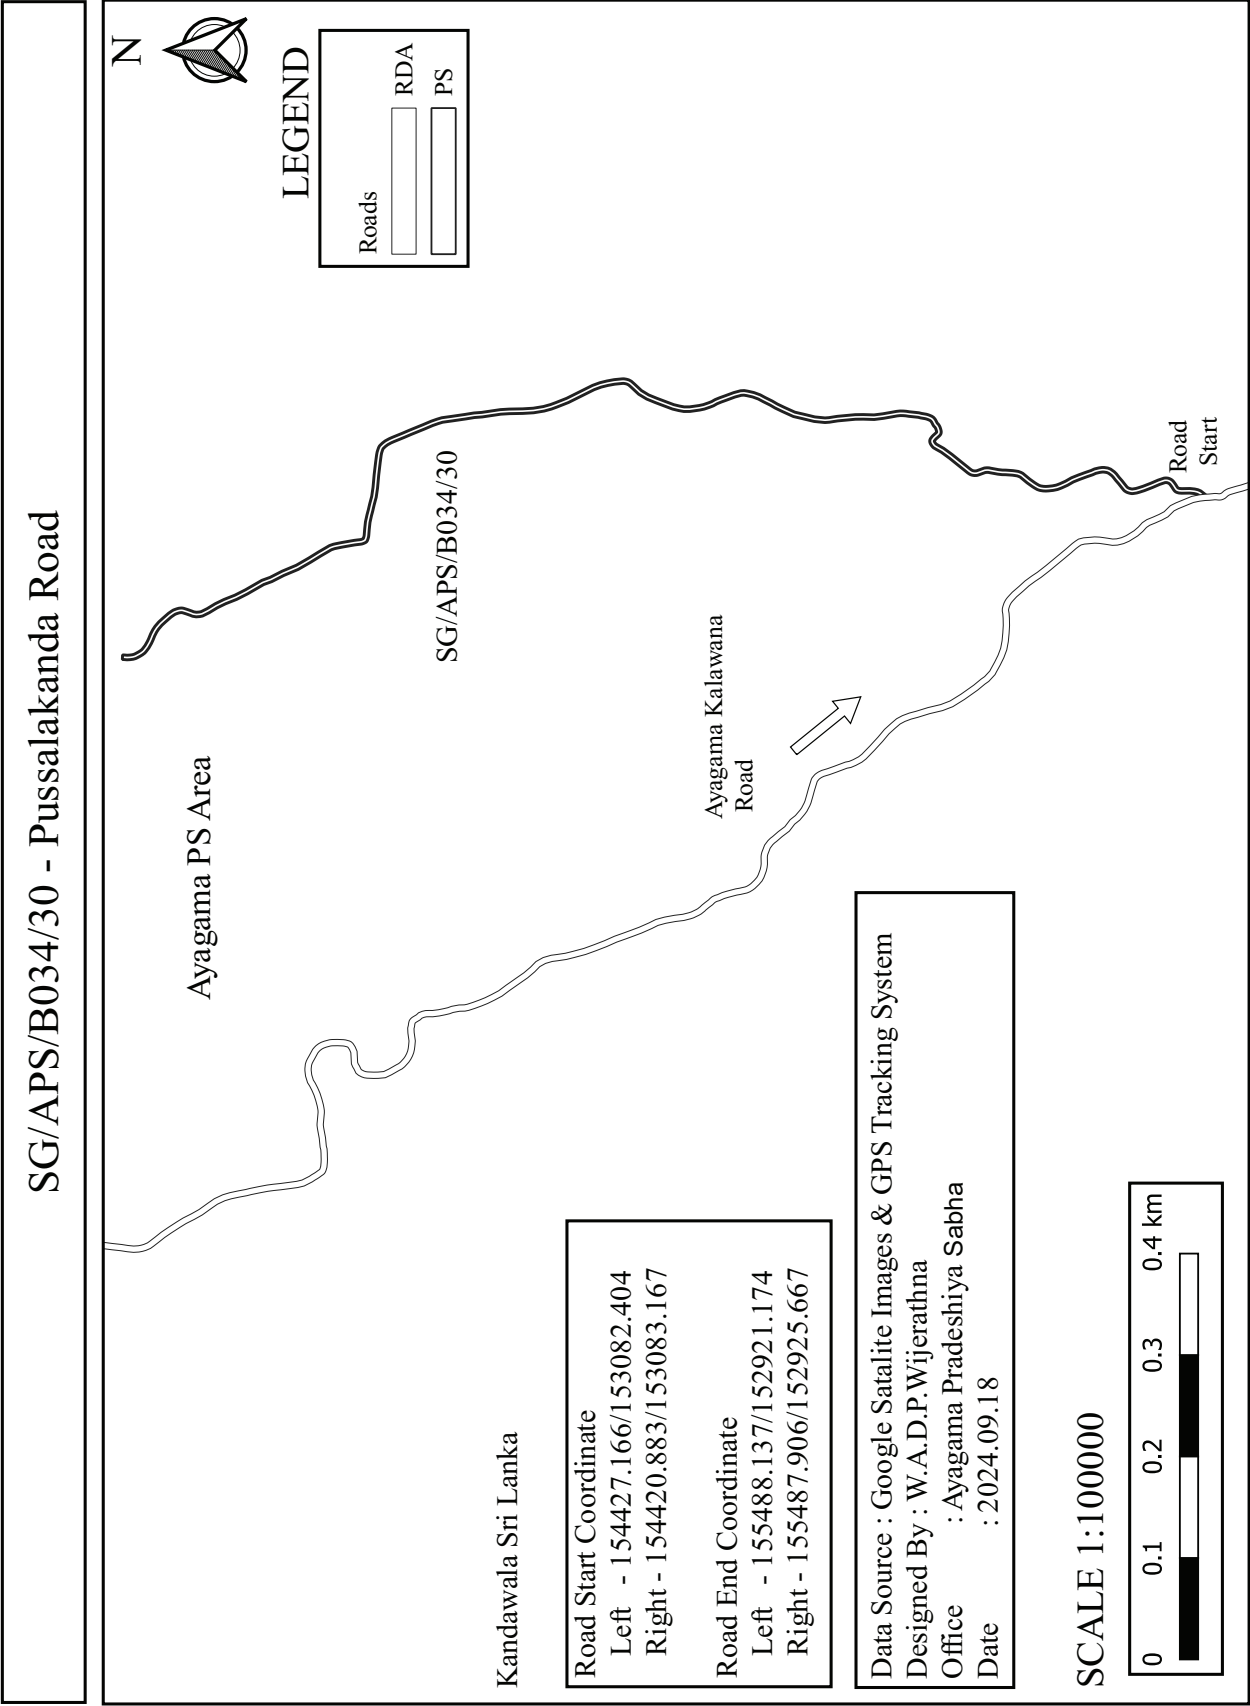


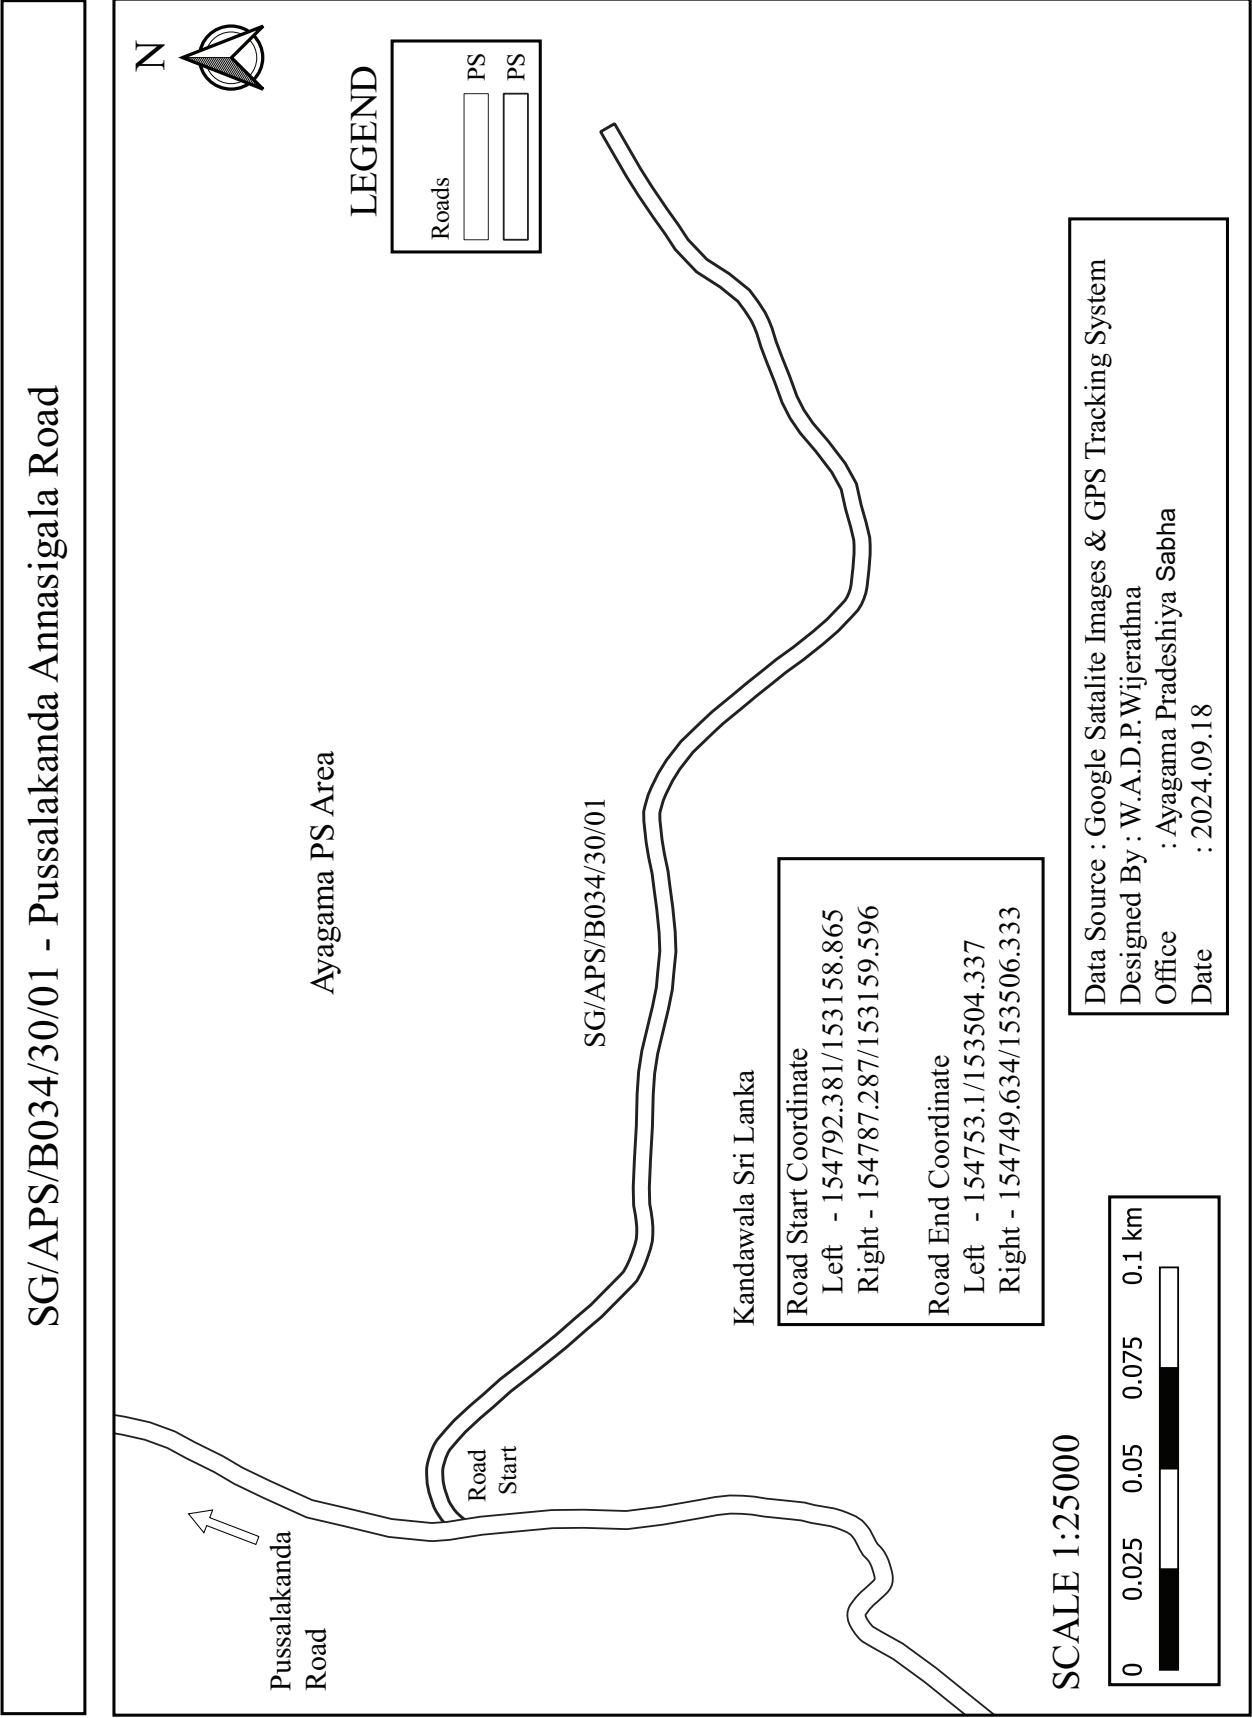


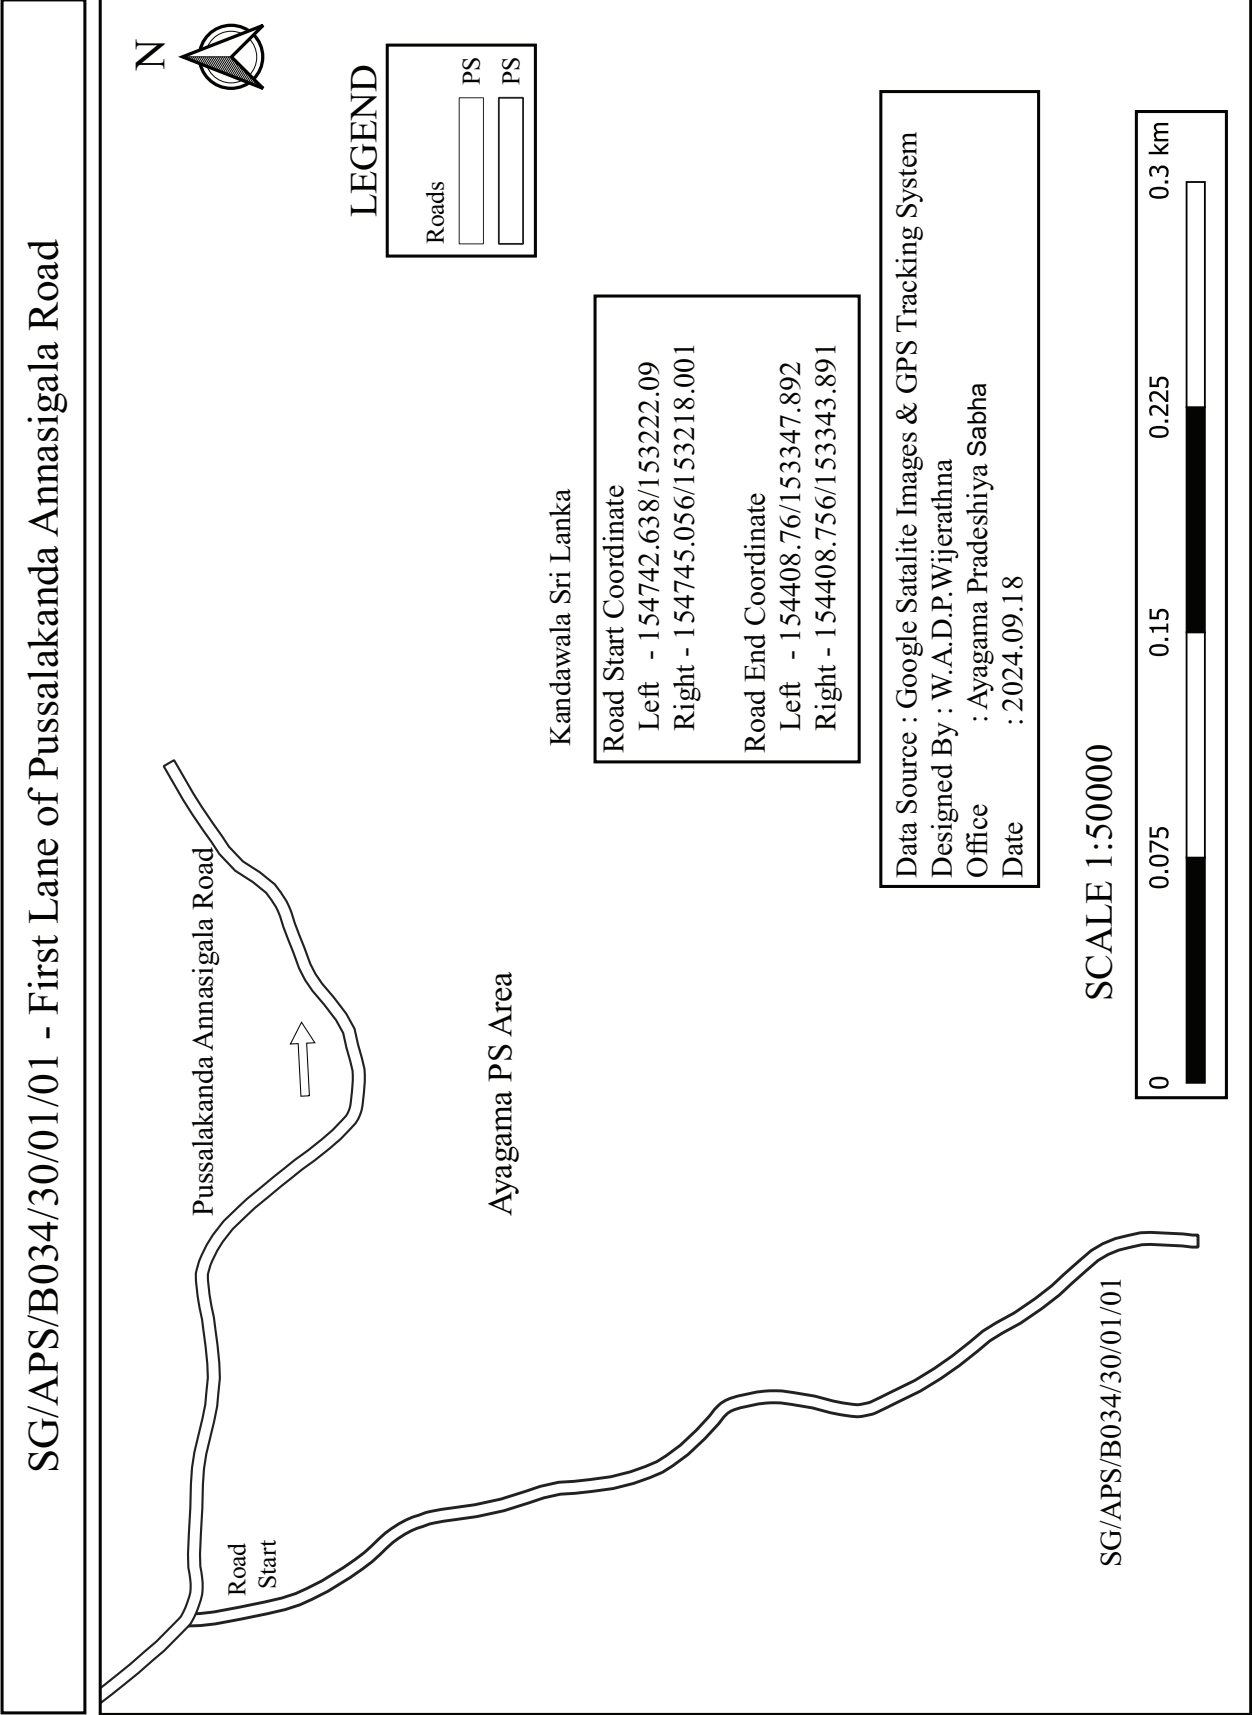


SG/APS/B034/30/02 - Pussalakanda Community Hall Road

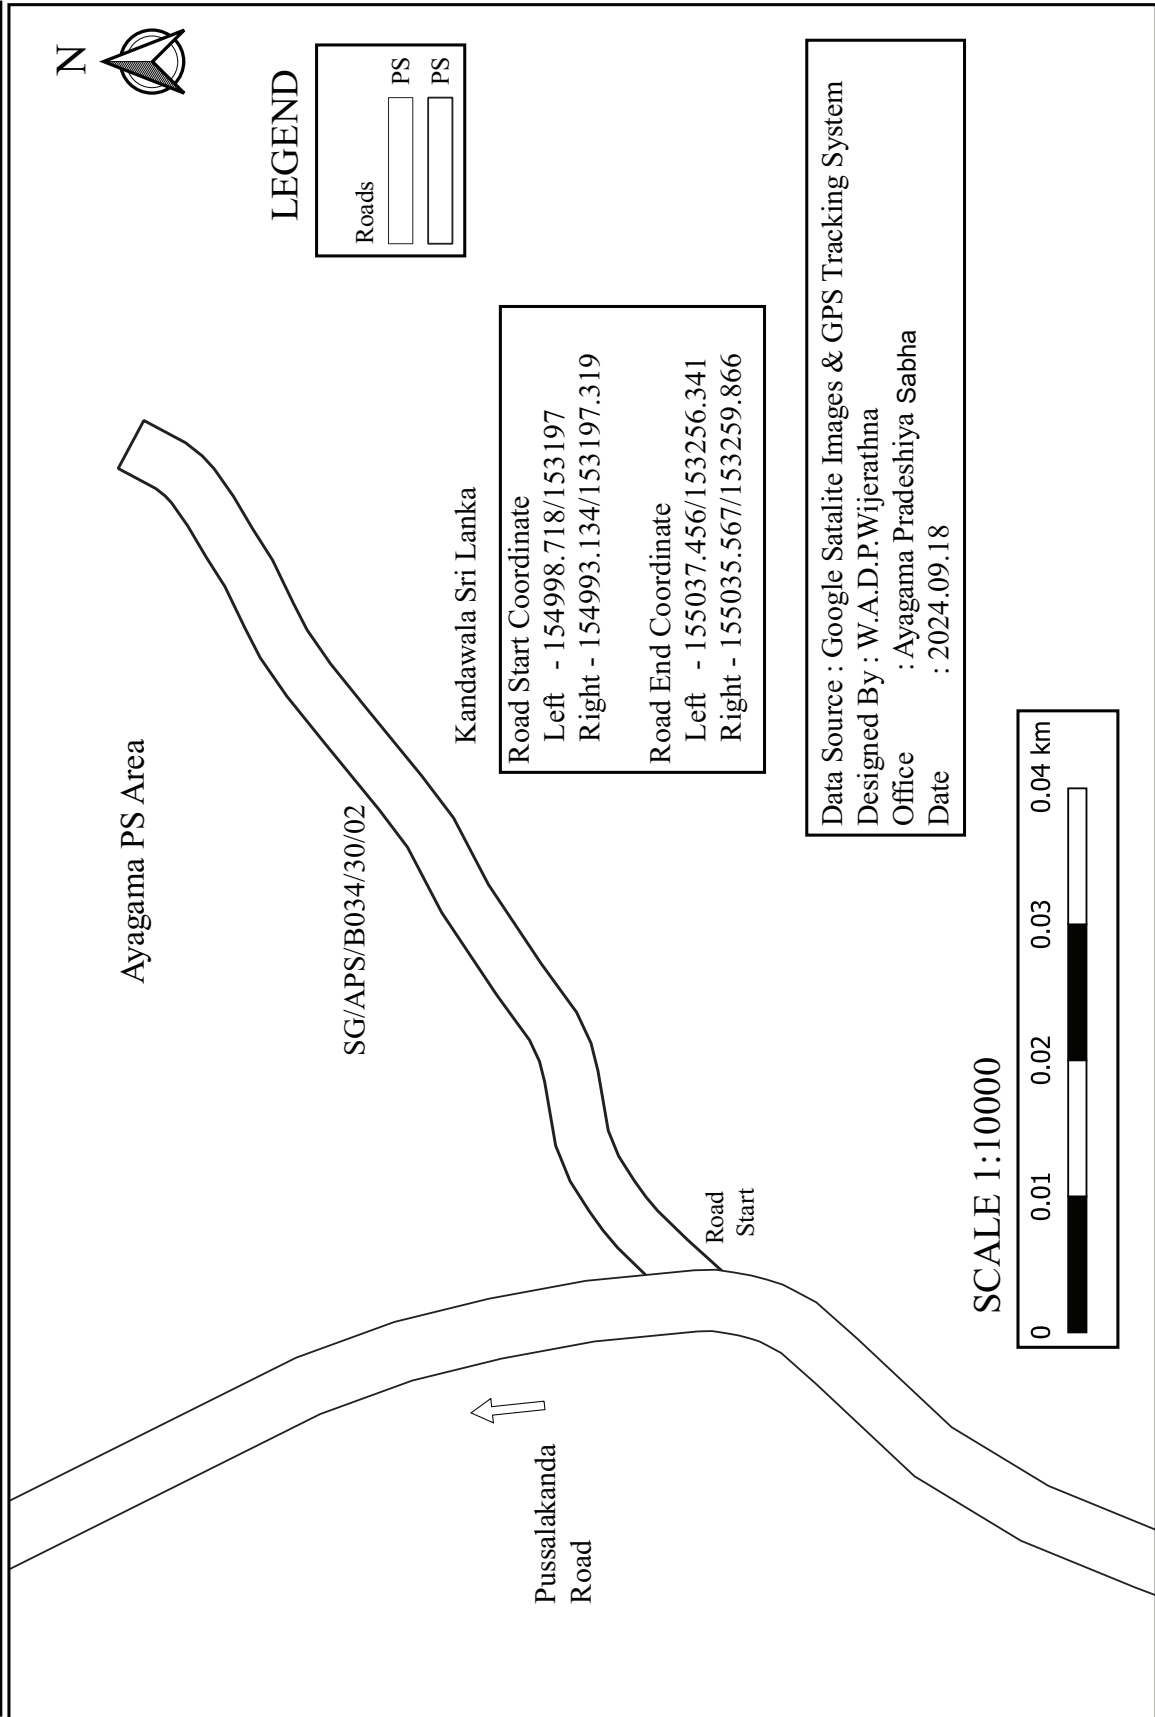


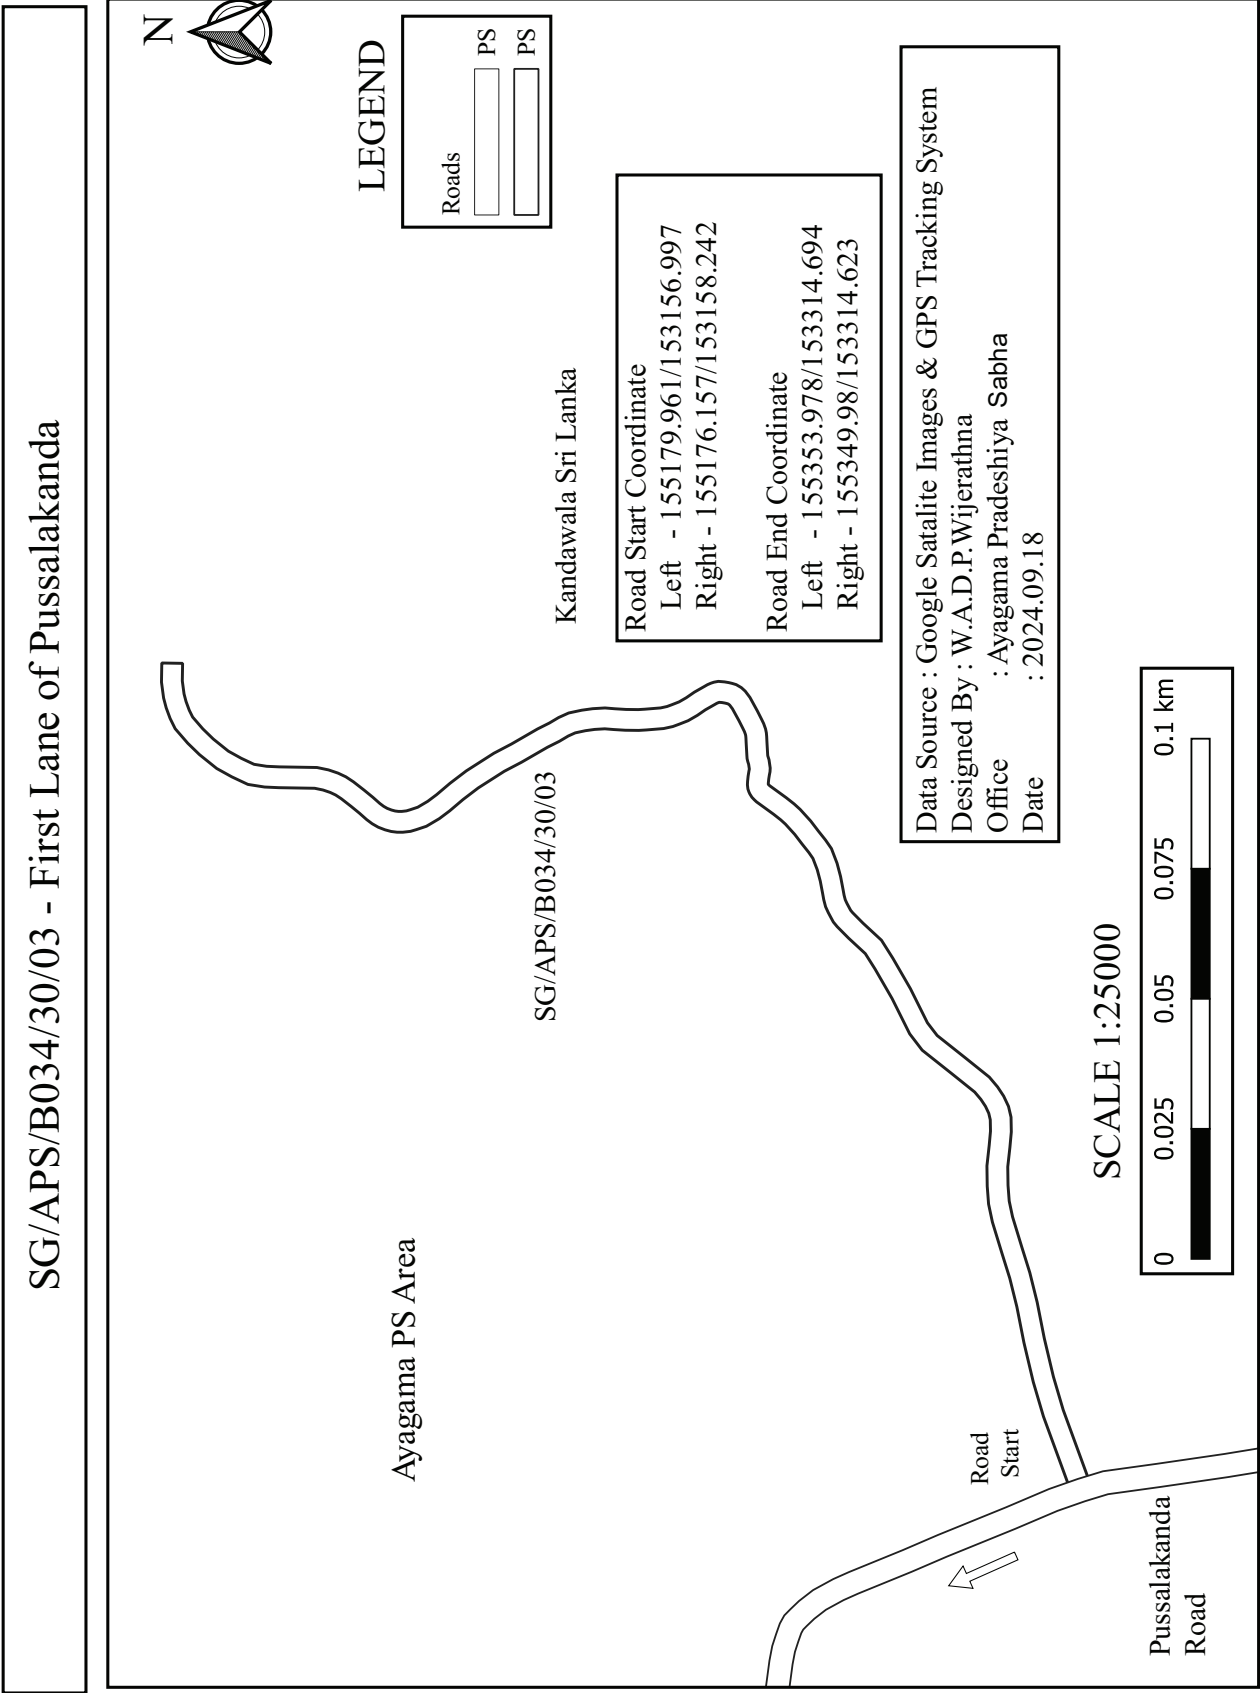


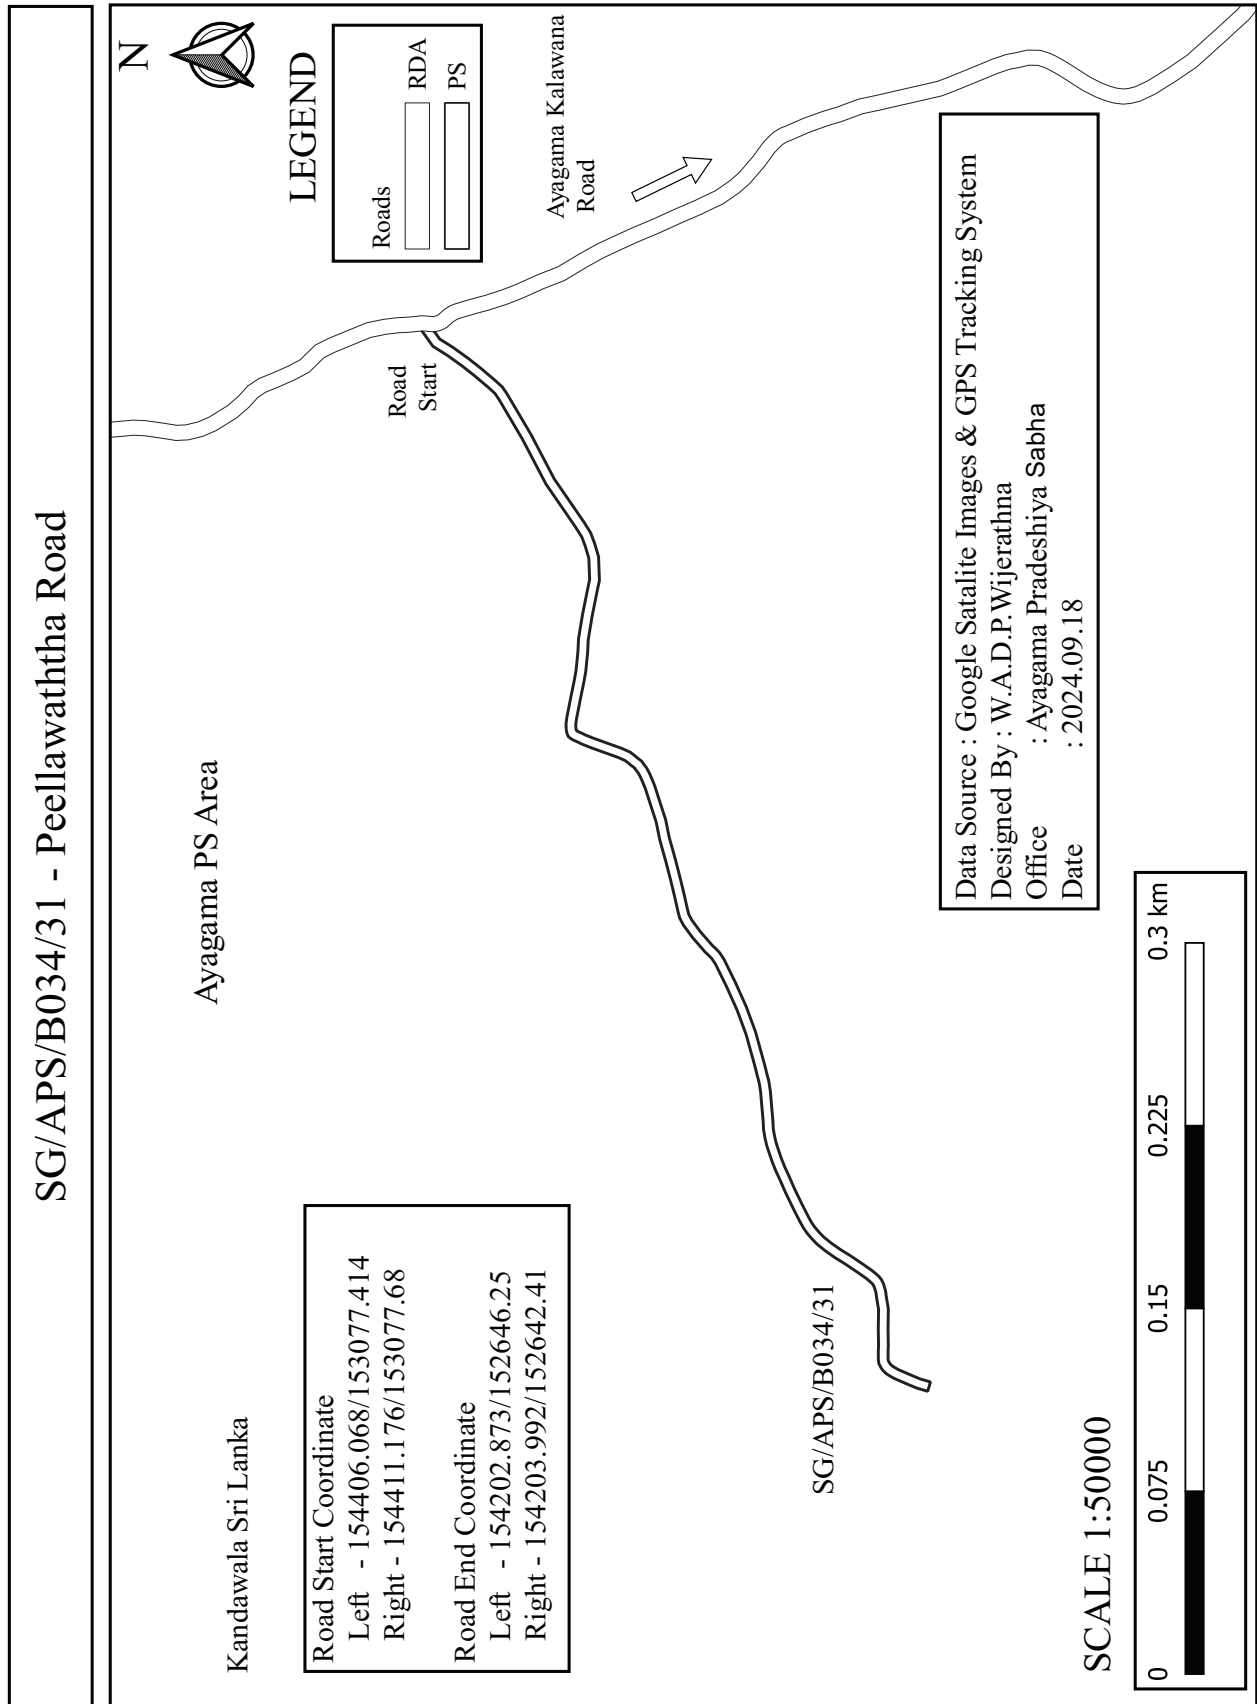

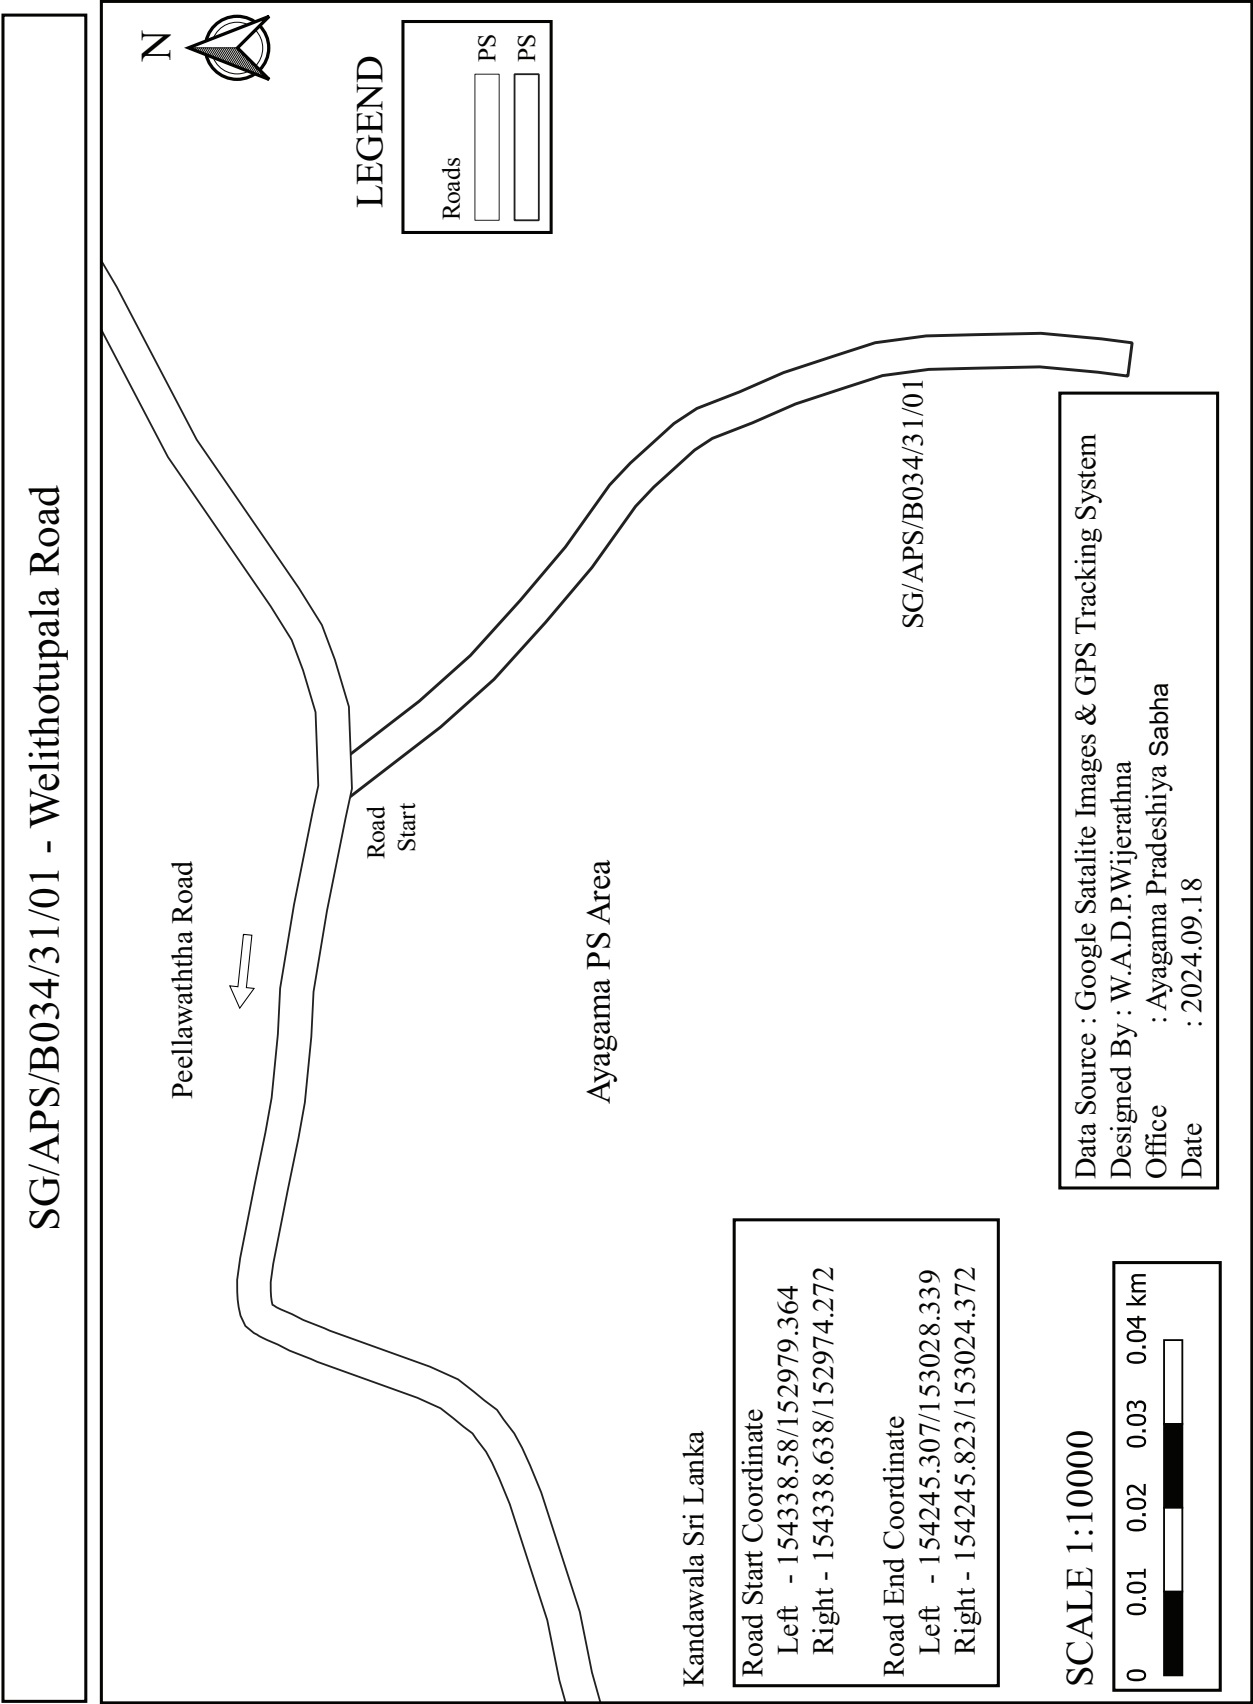



SG/APS/B034/31/02 - First Lane of Peellawaththa Road

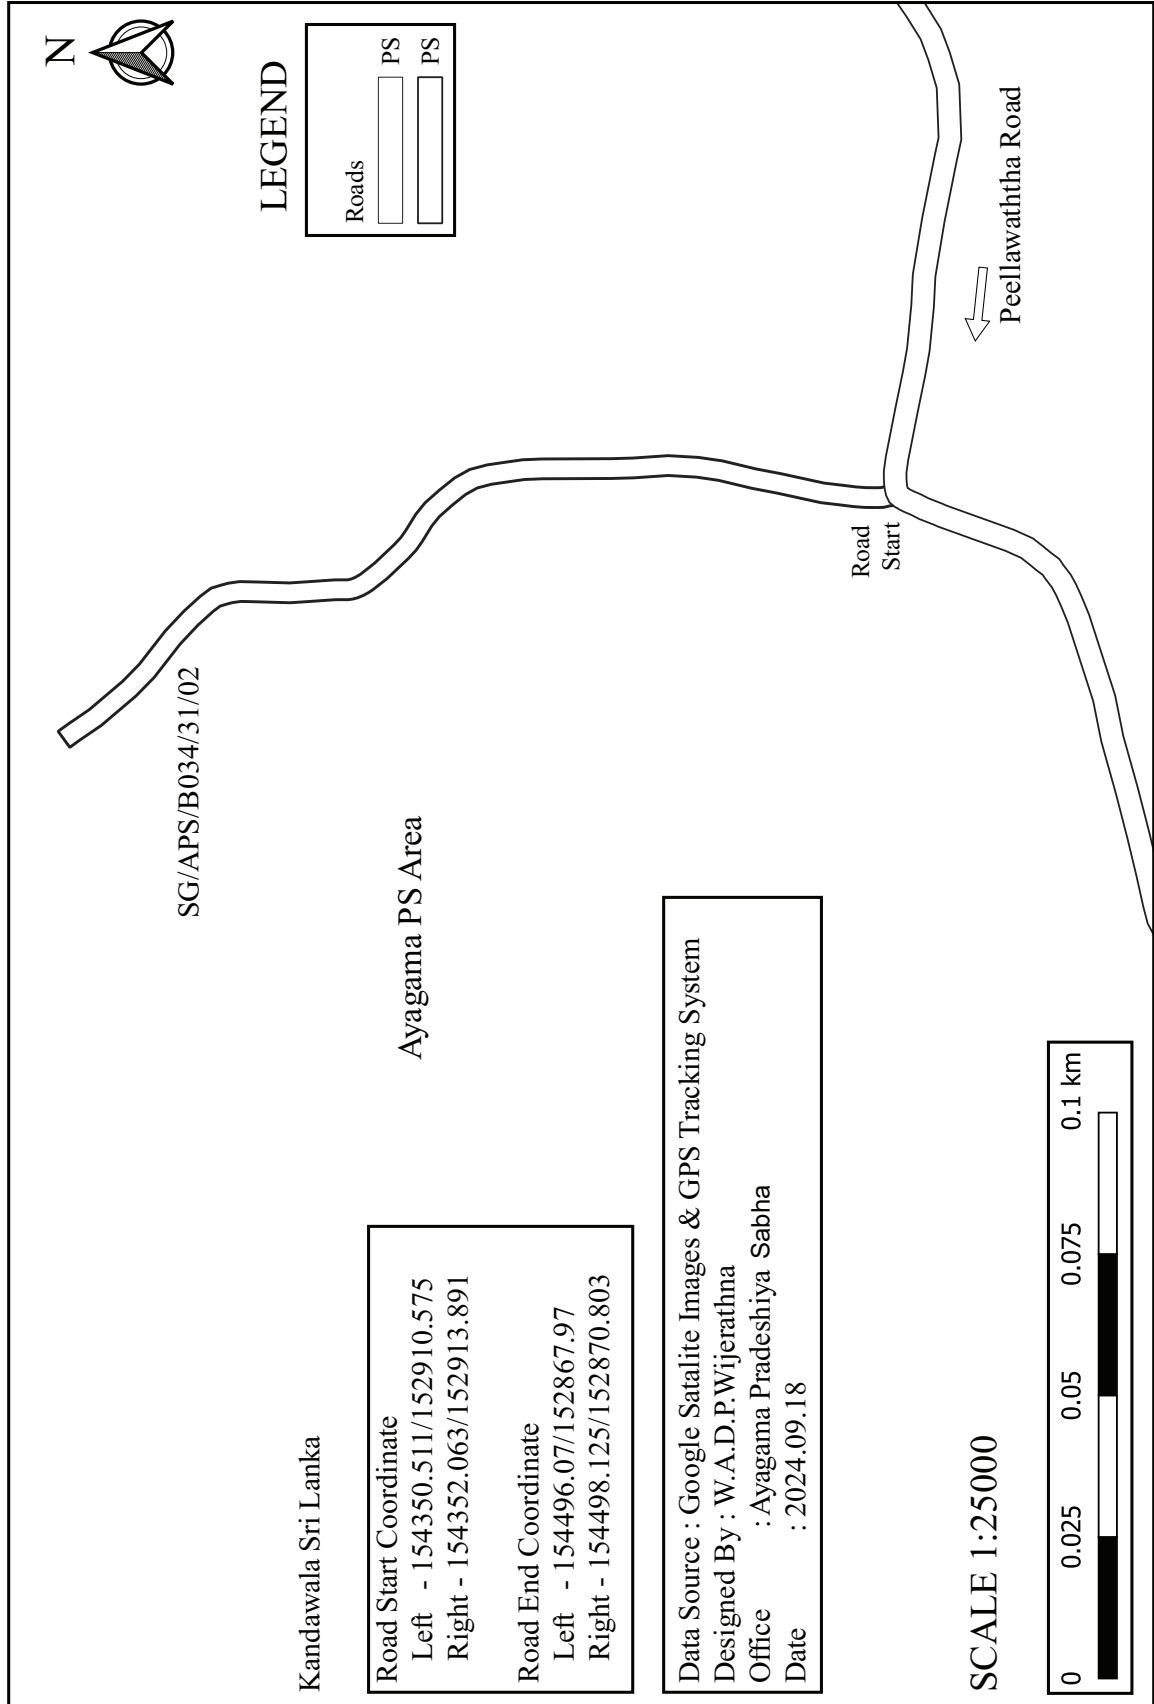


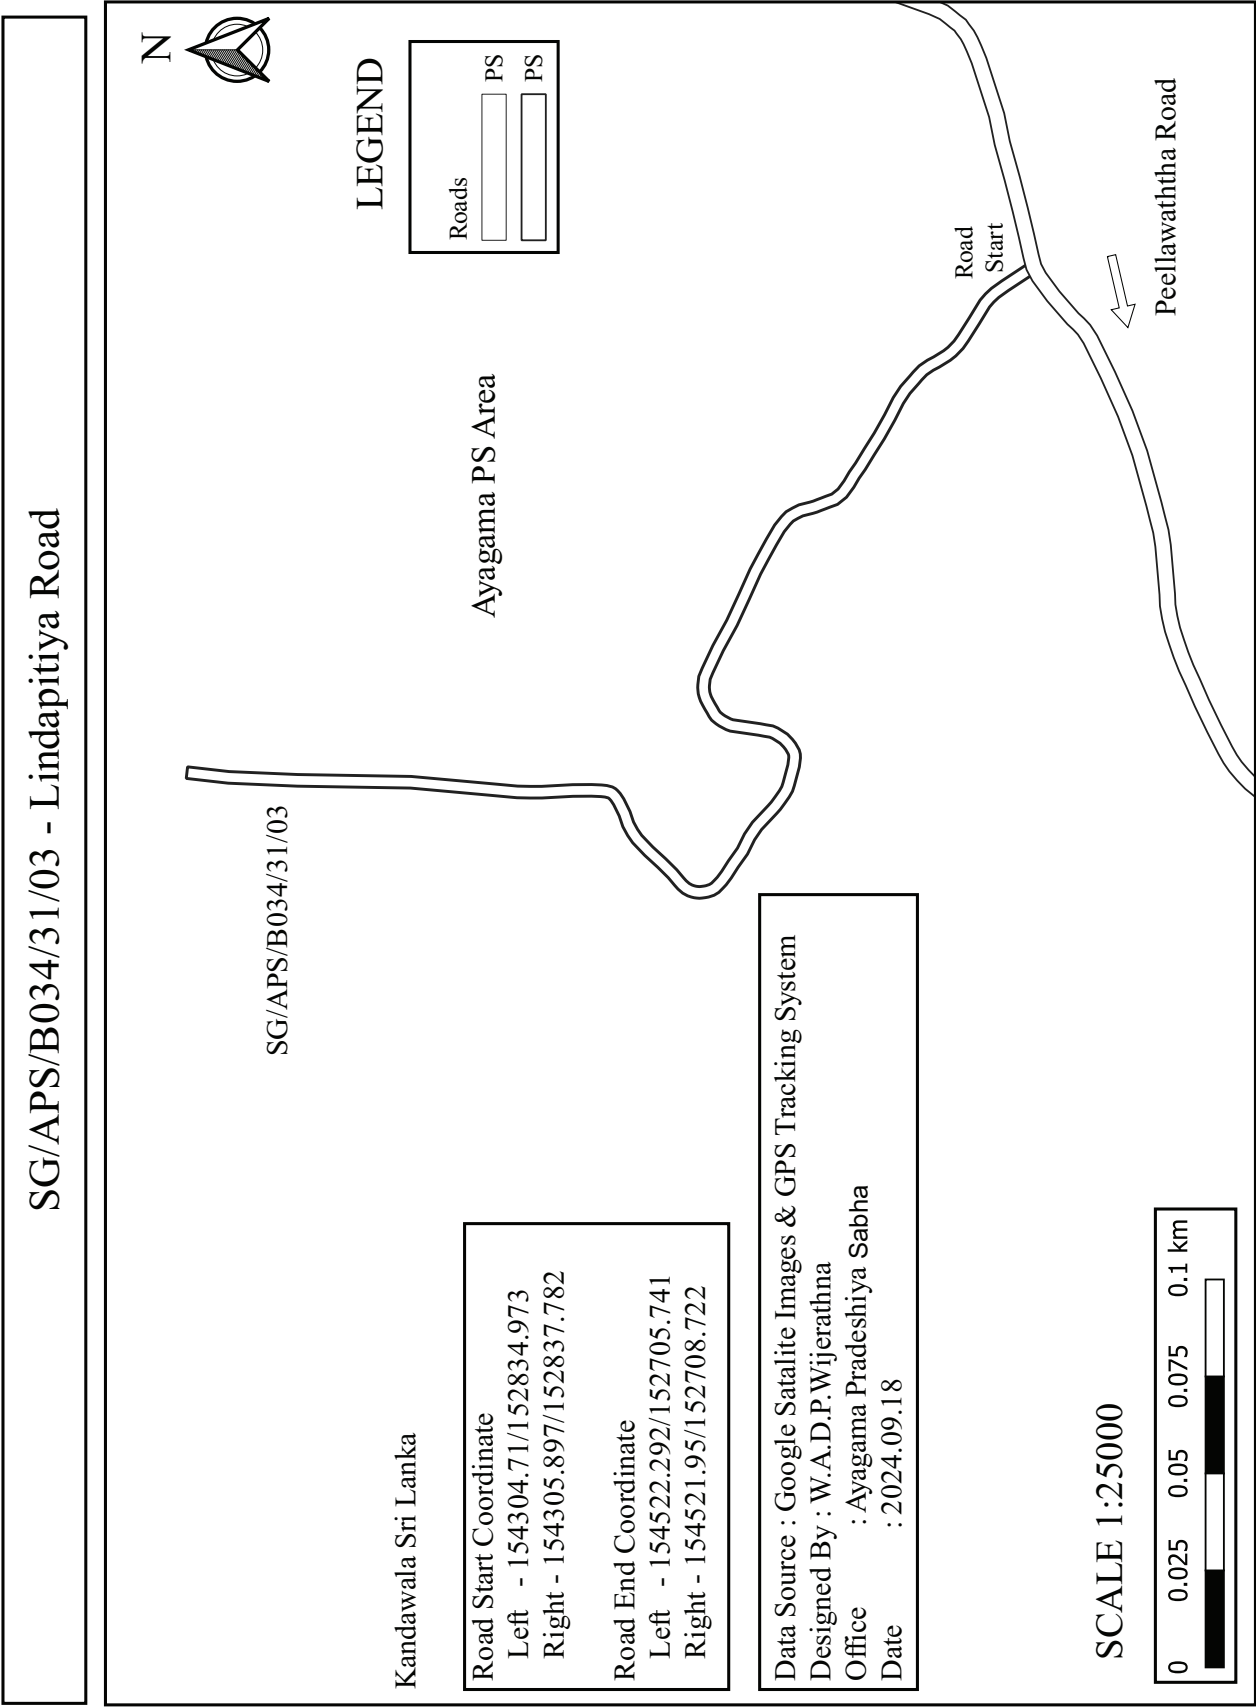



SG/APS/B034/31/03/01 - Lindapitiya Aranya Road

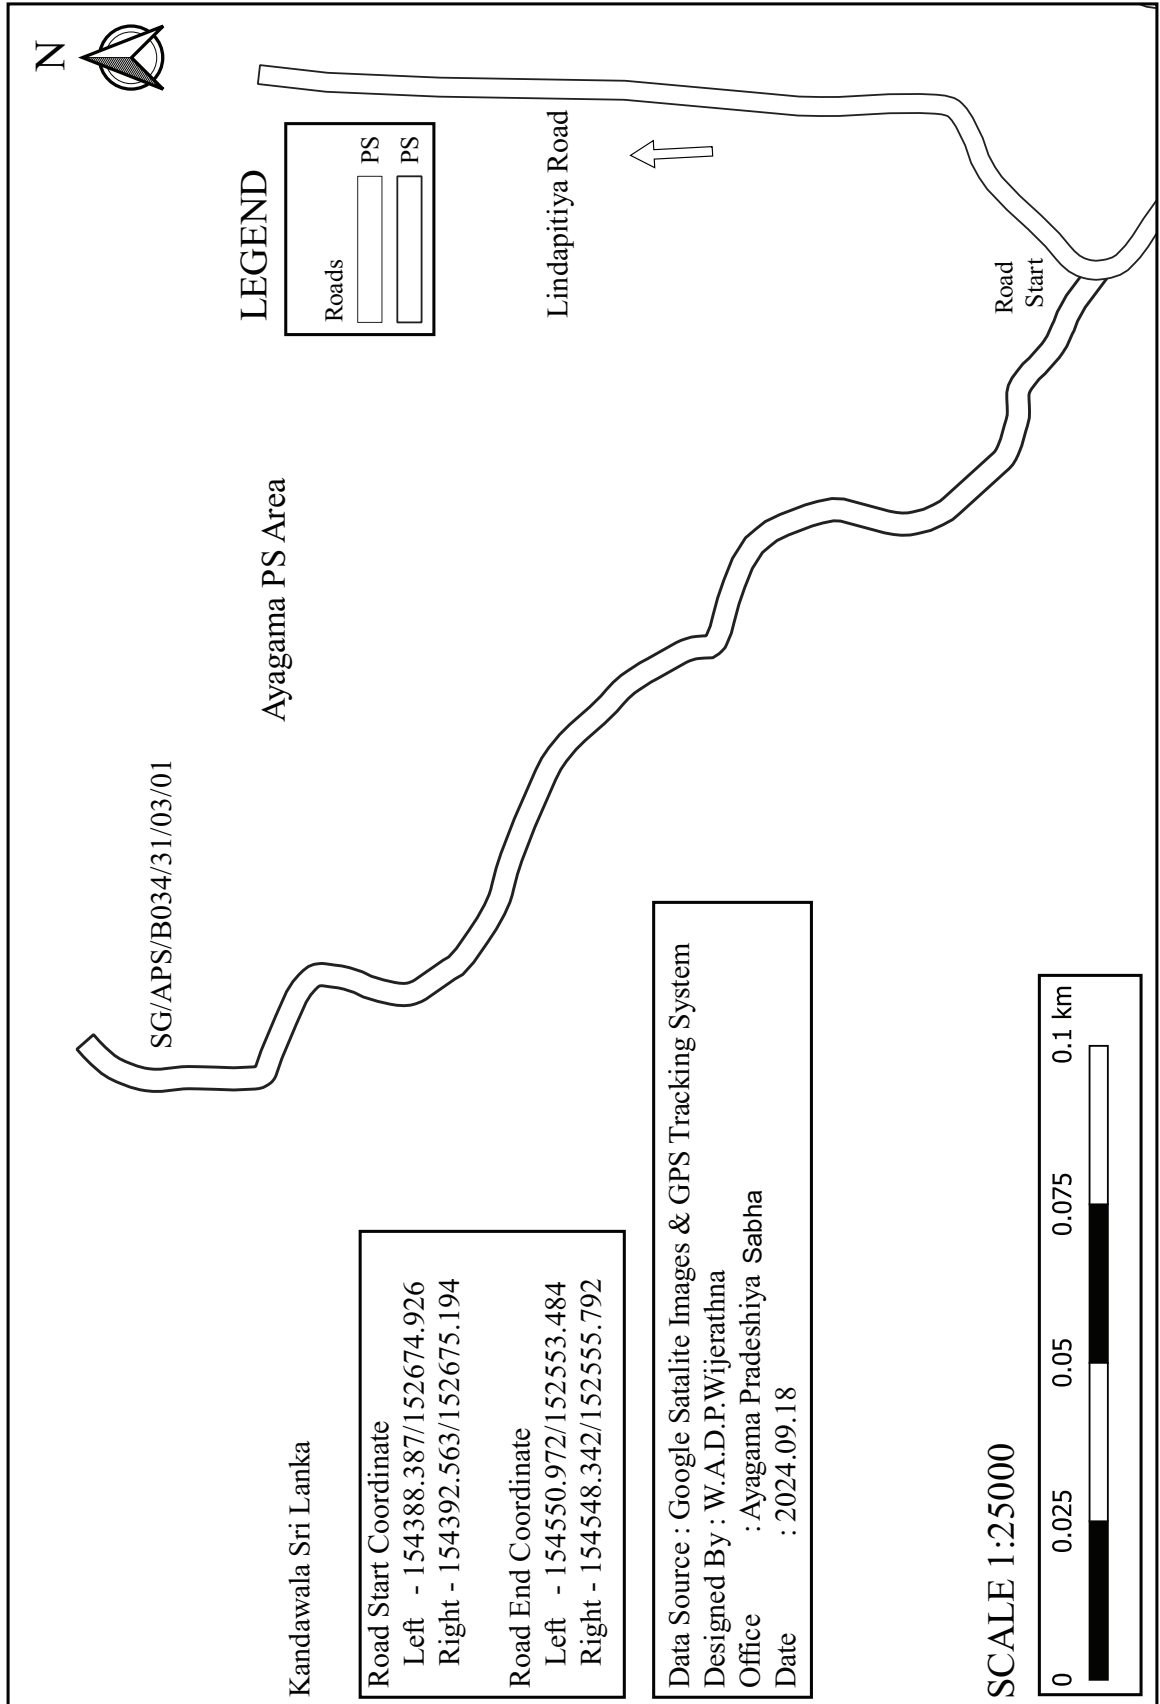


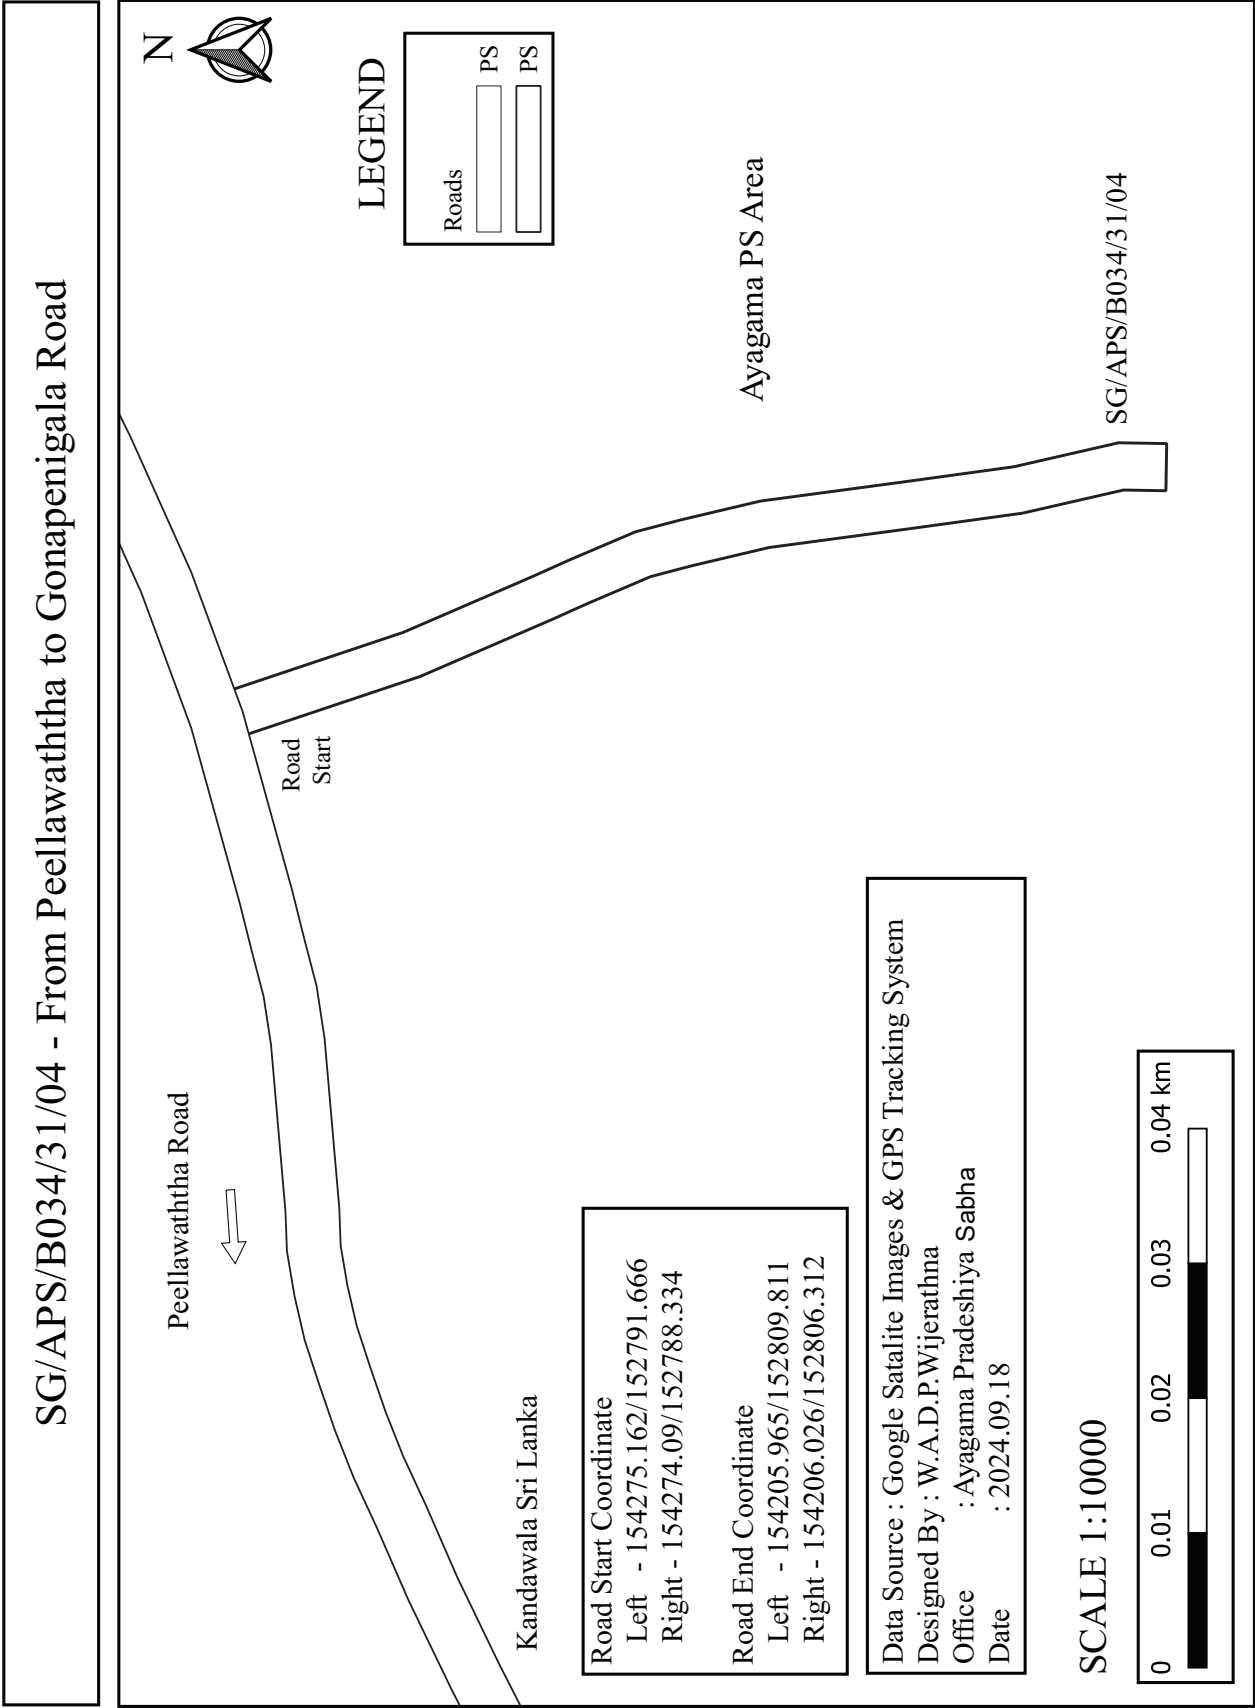

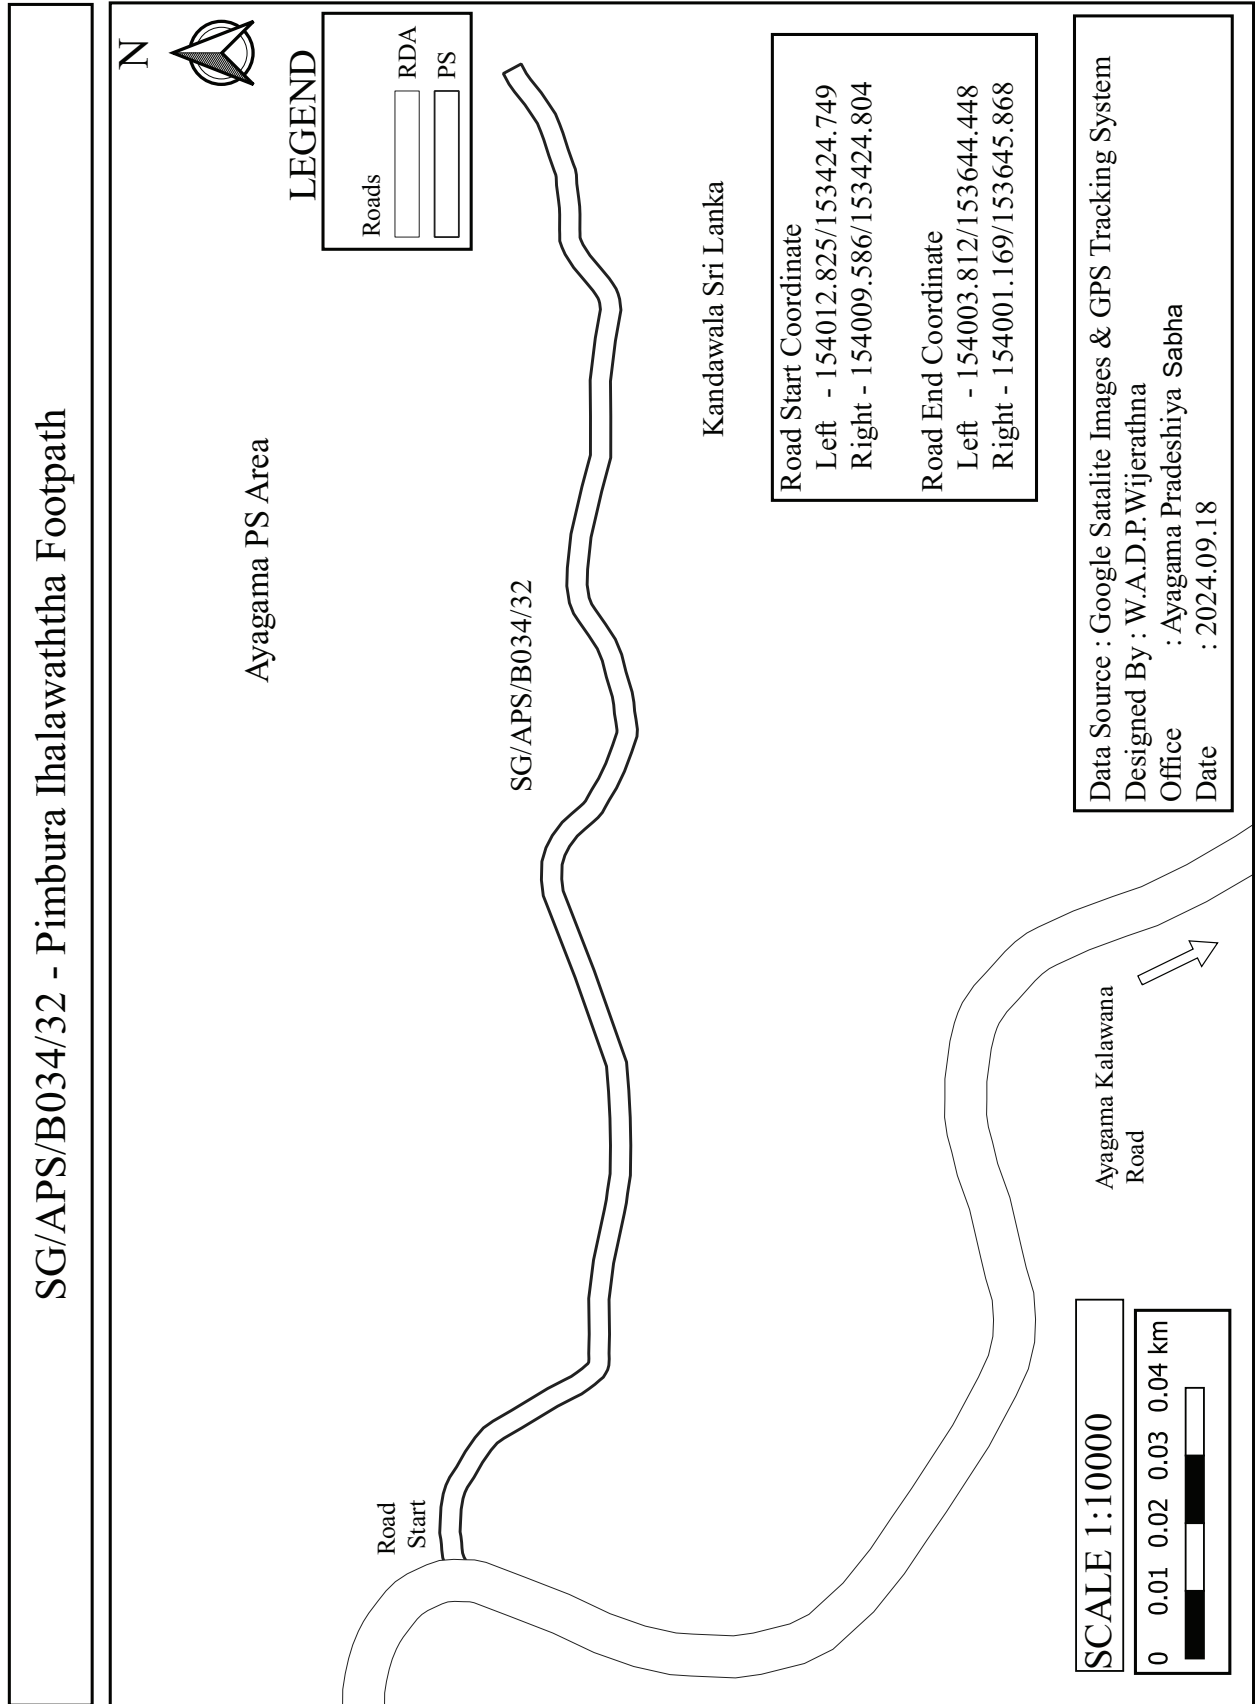


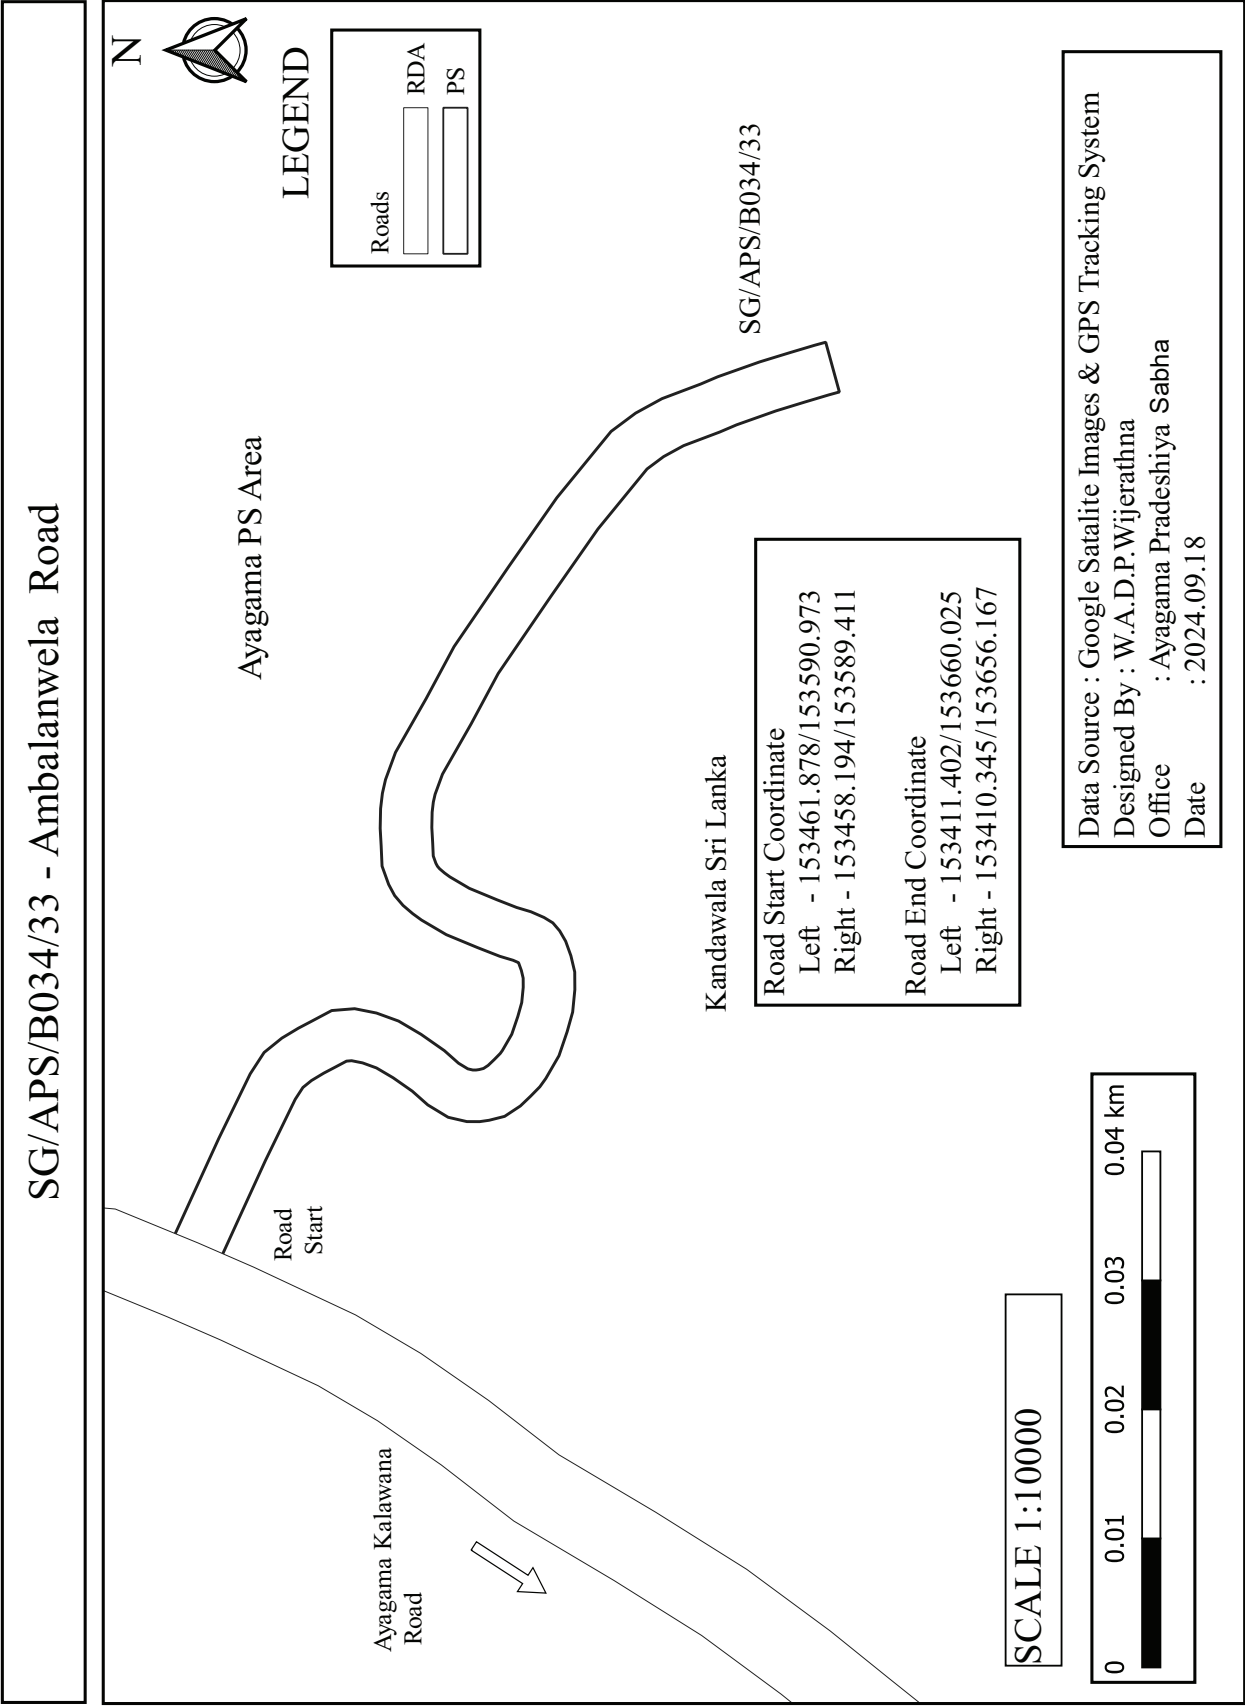


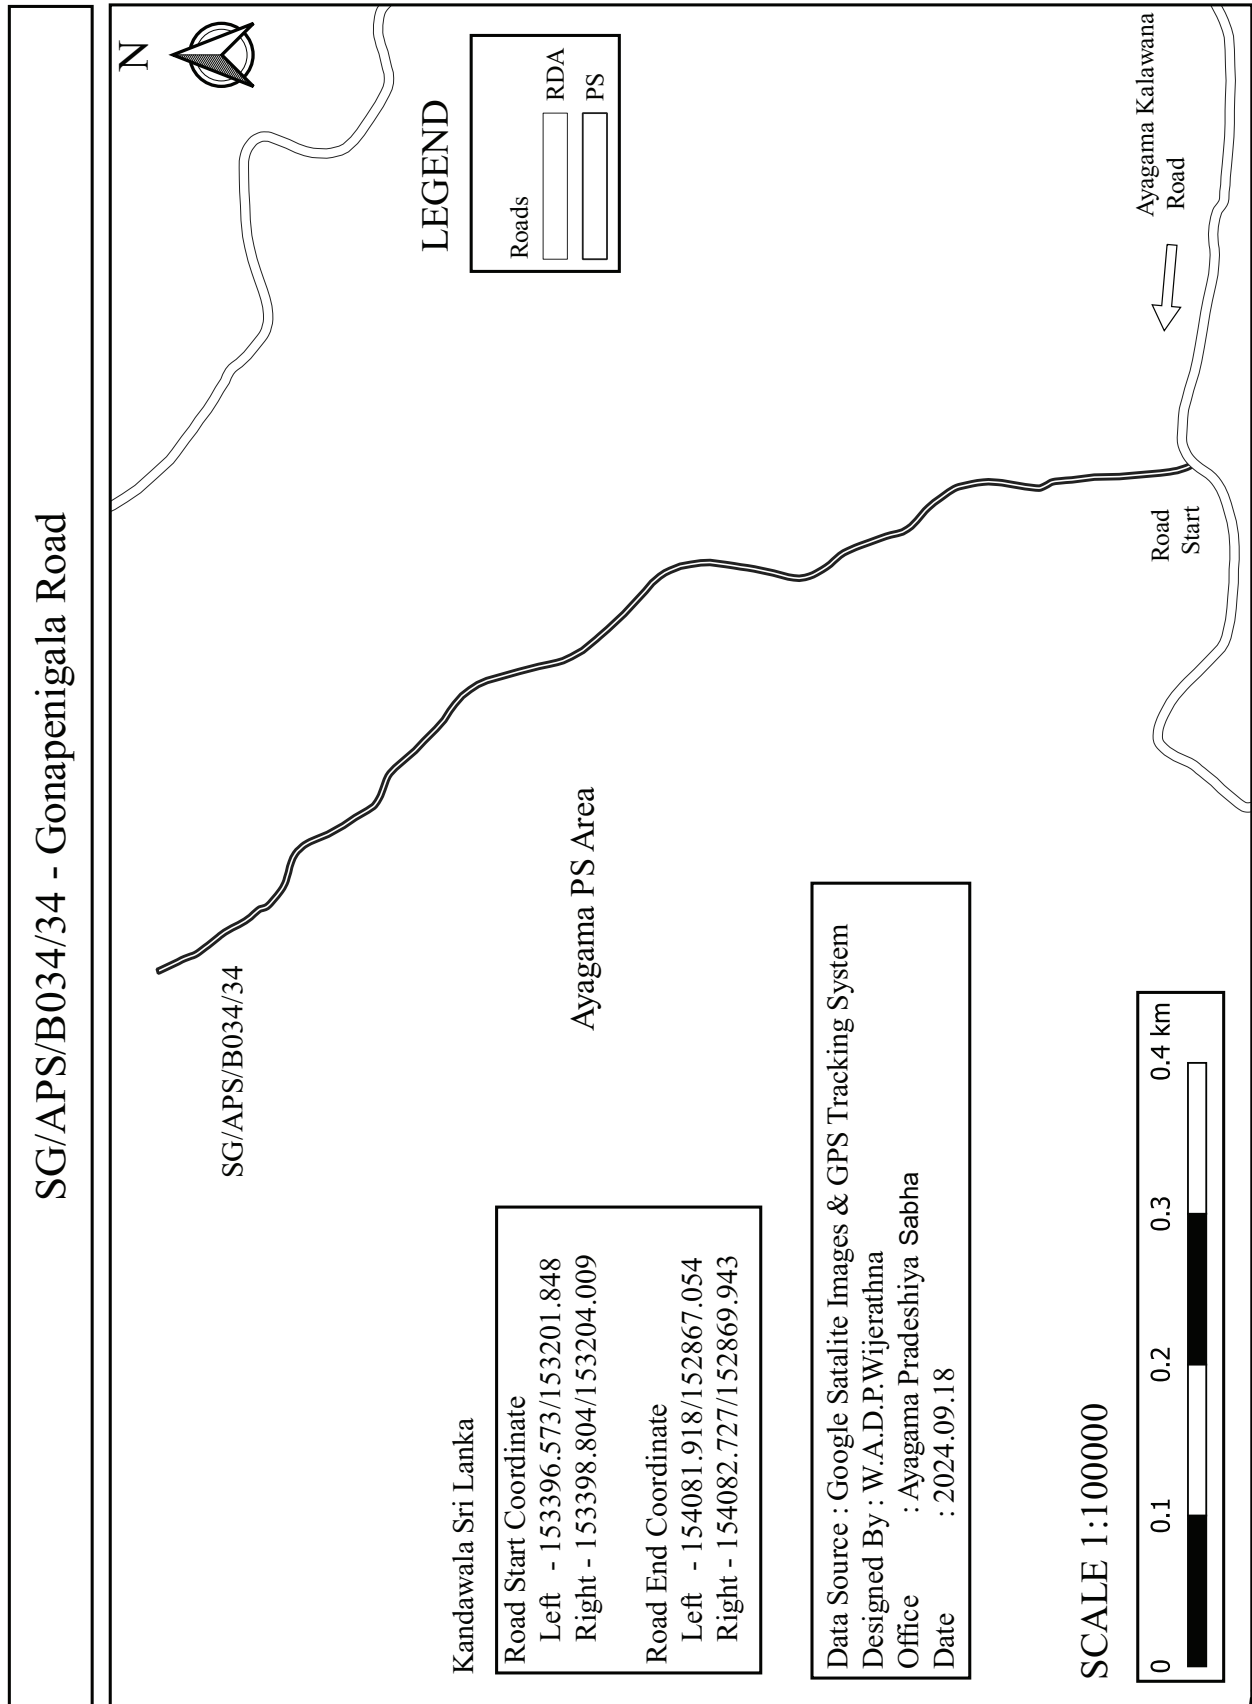

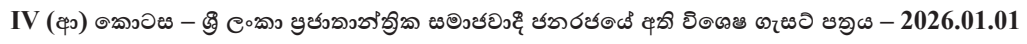



SG/APS/B034/35/01 - Manakanda Road

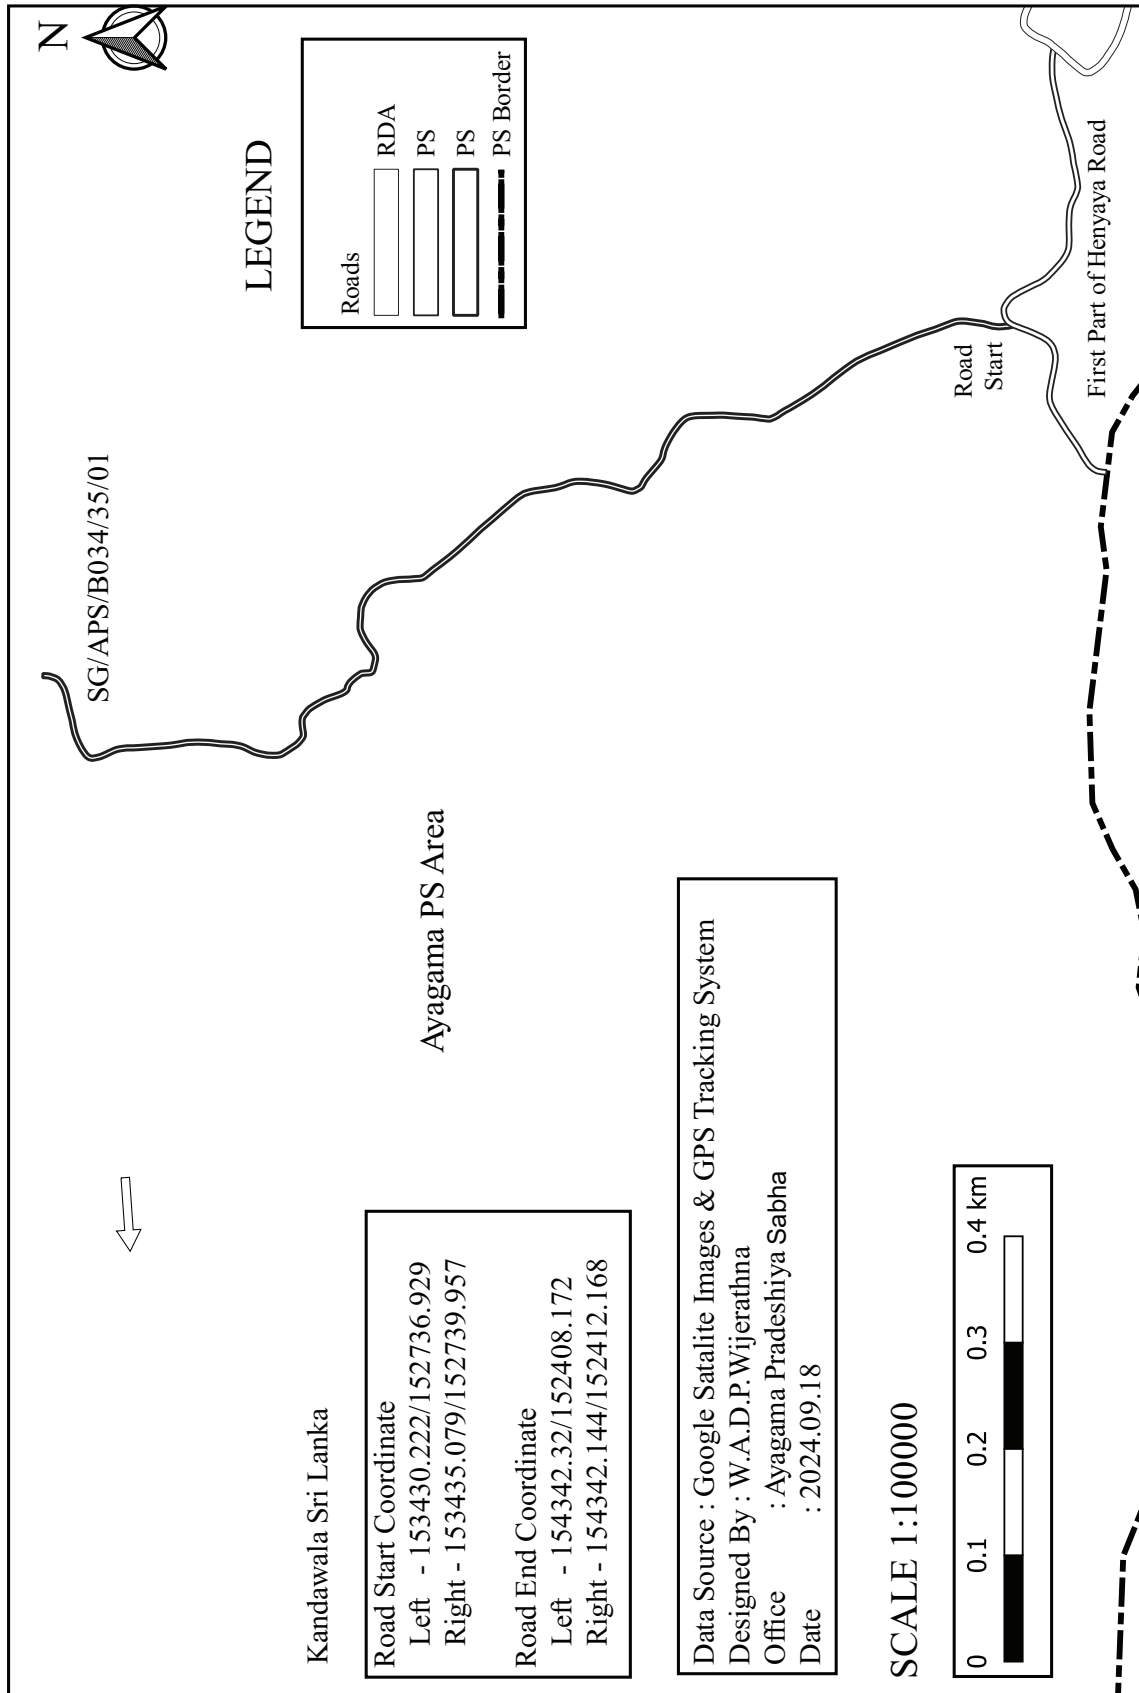

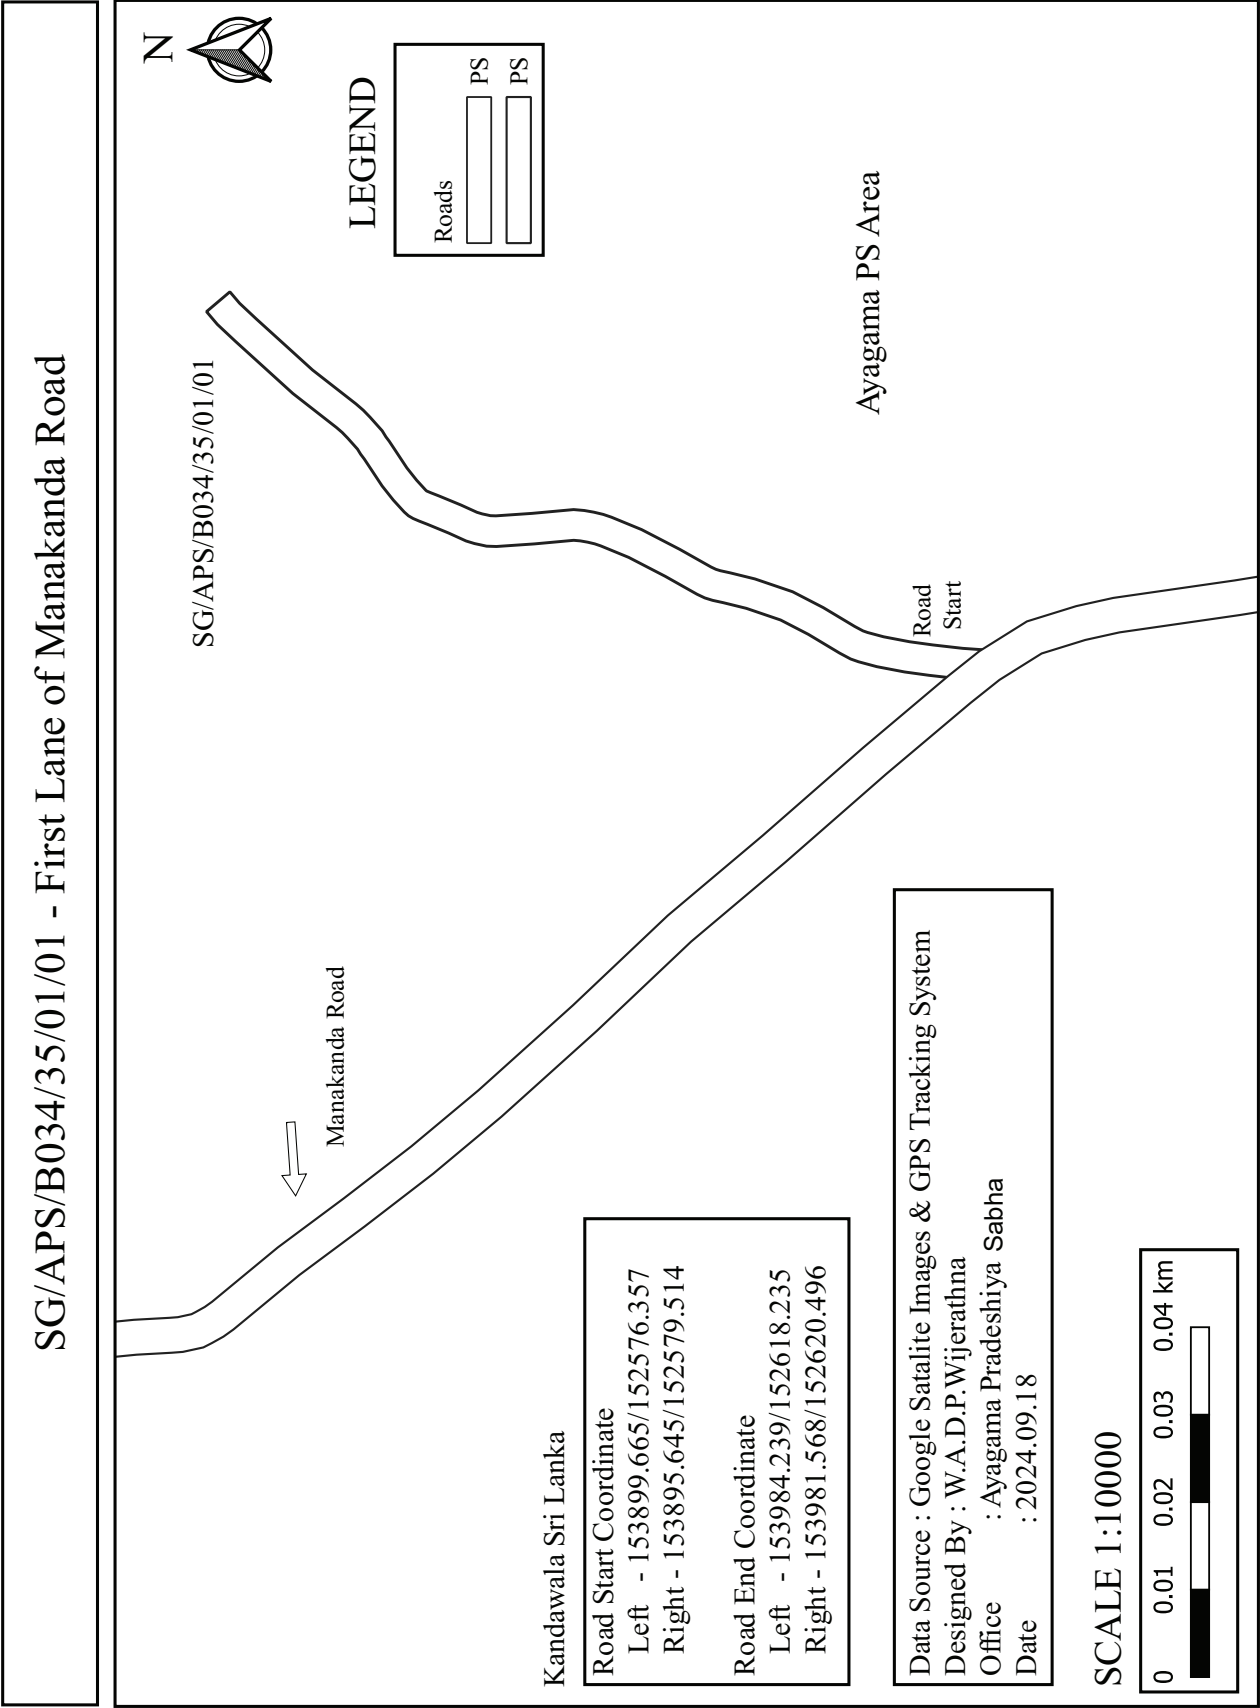



SG/APS/B034/35/01/02 - Second Lane of Manakanda Road

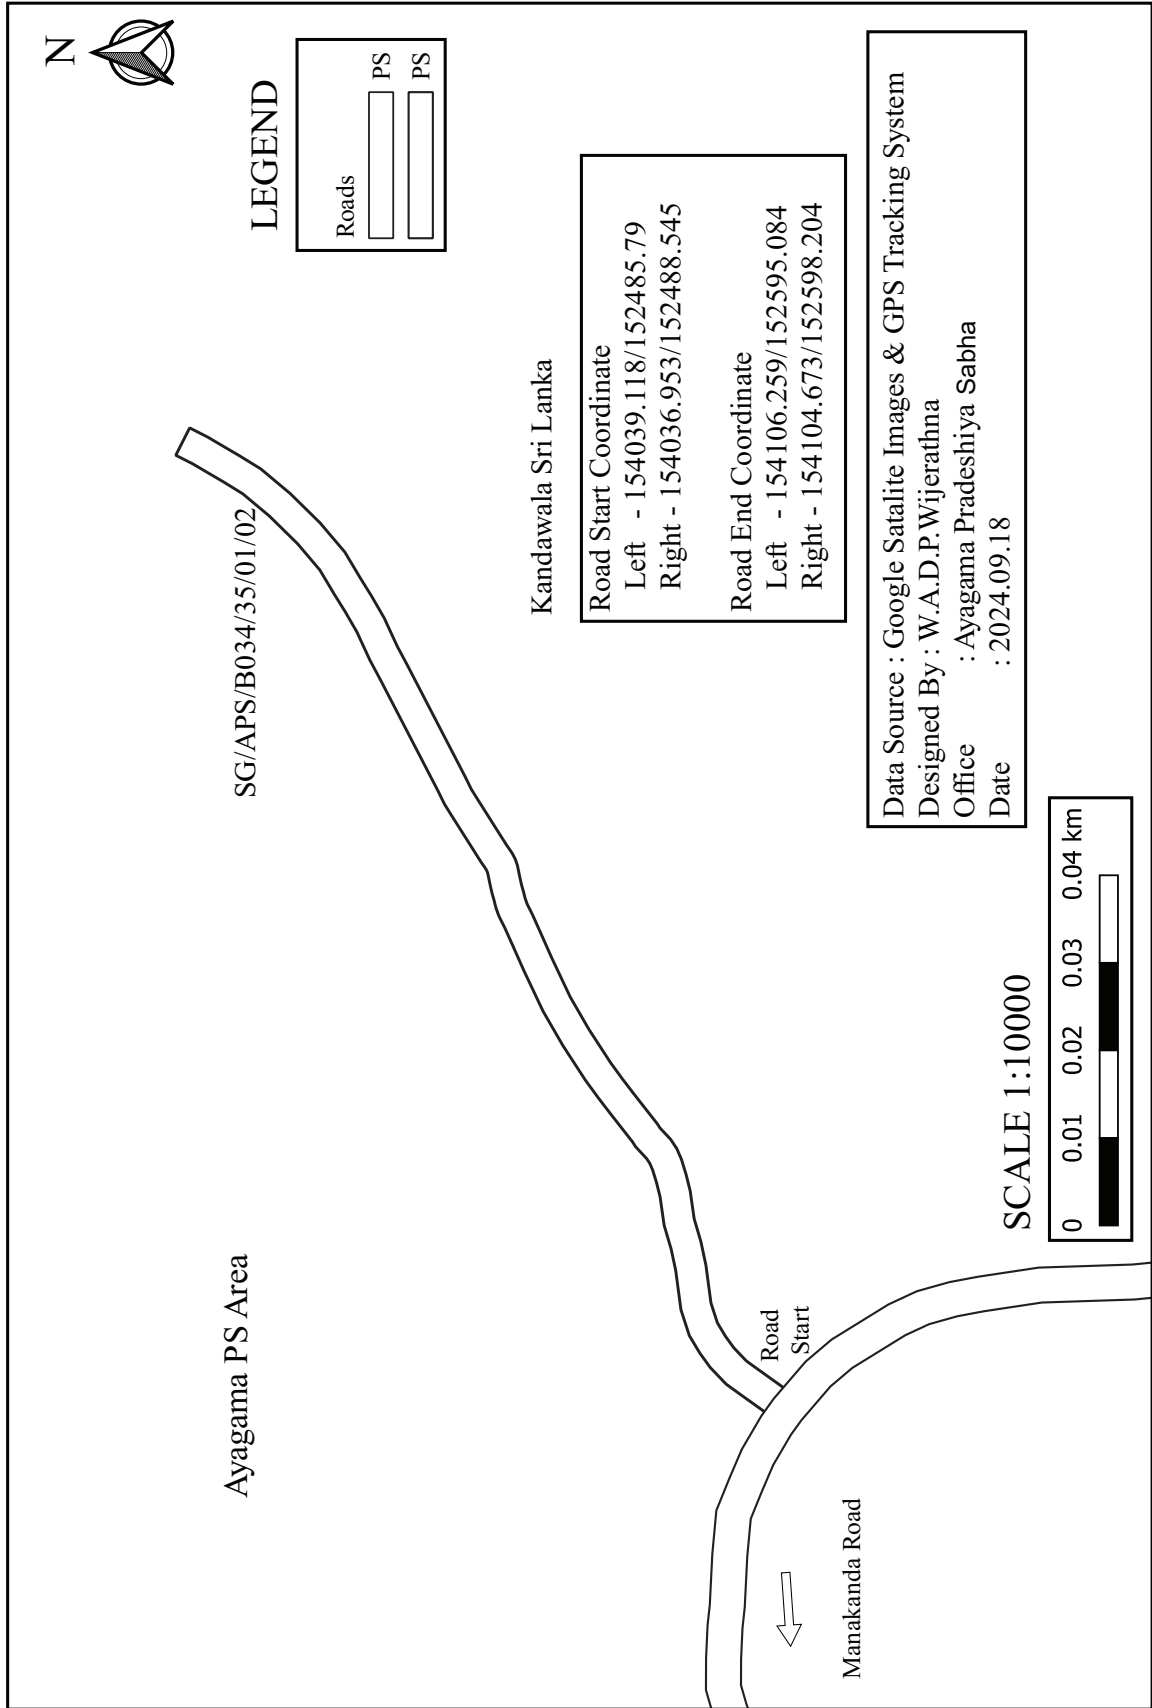

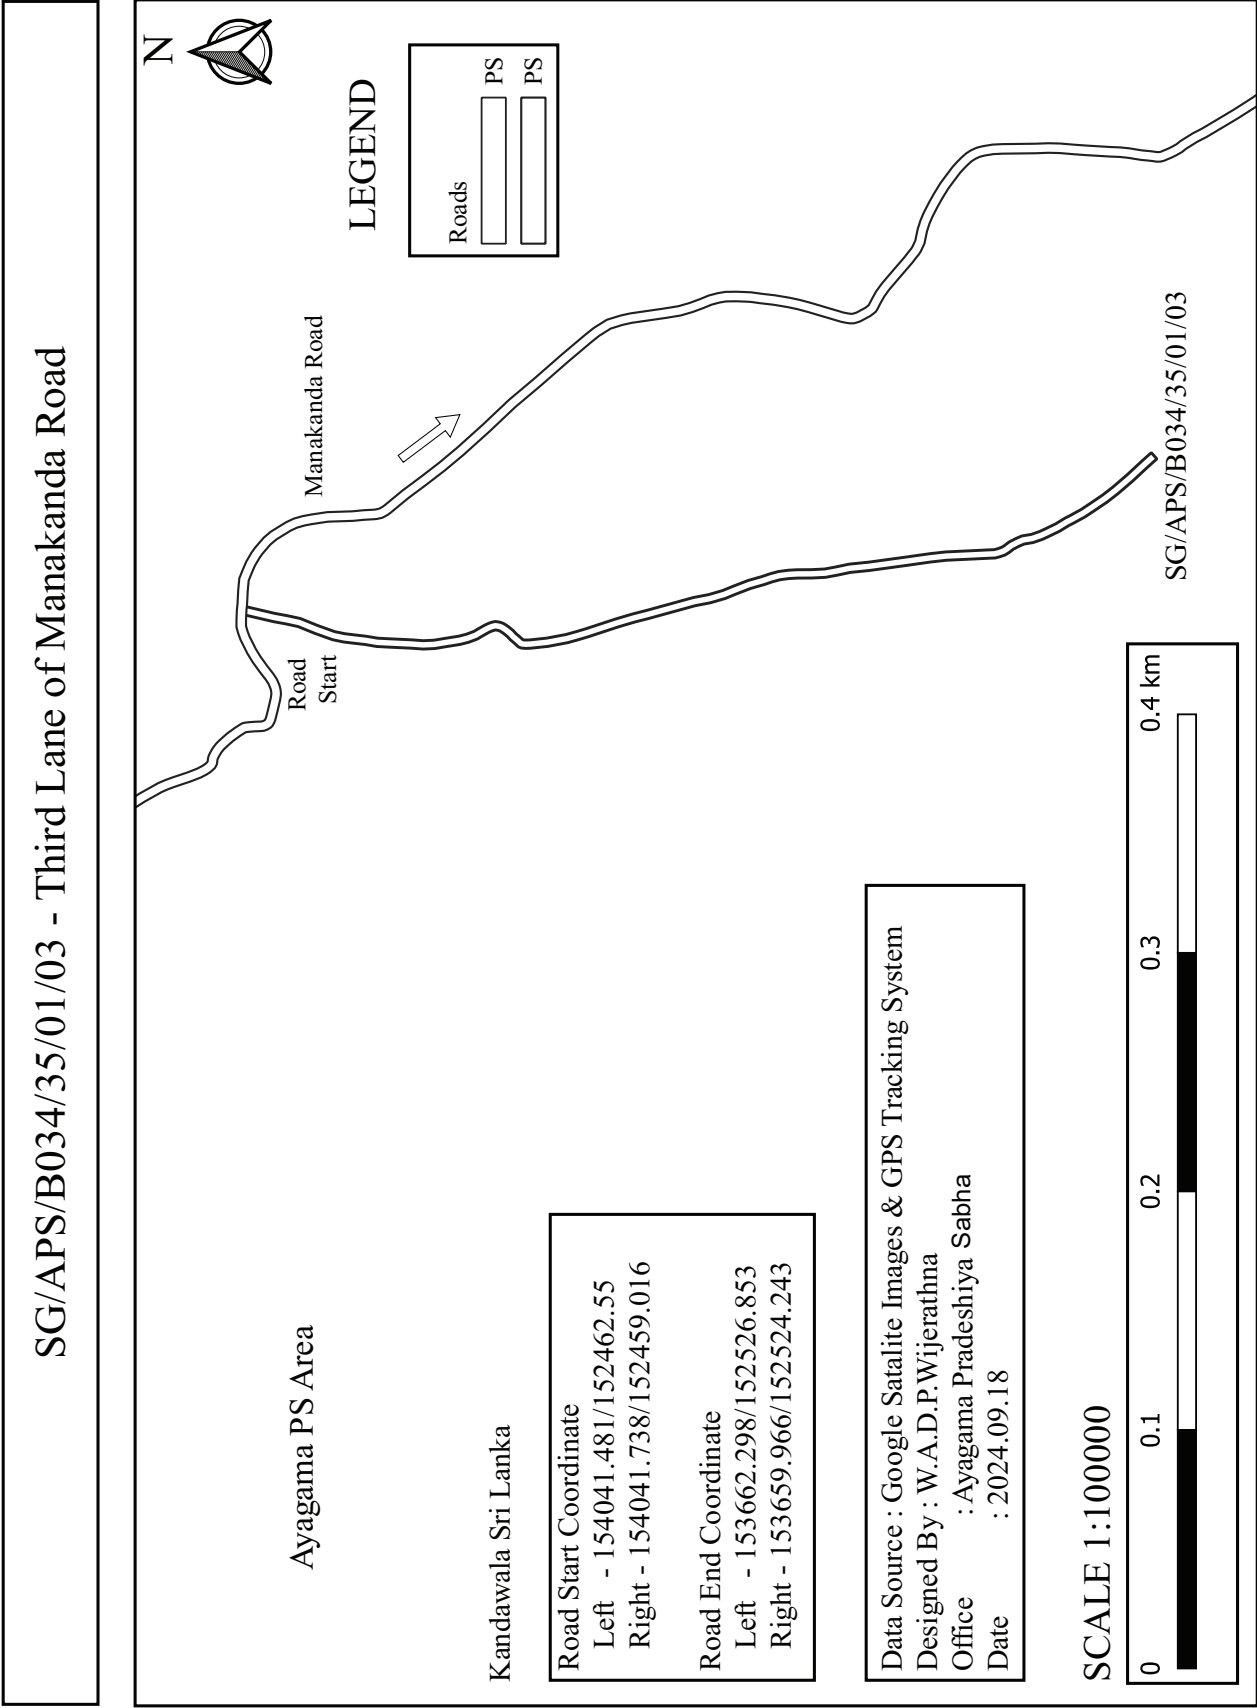



SG/APS/B034/35/01/04 - Fourth Lane of Manakanda Road

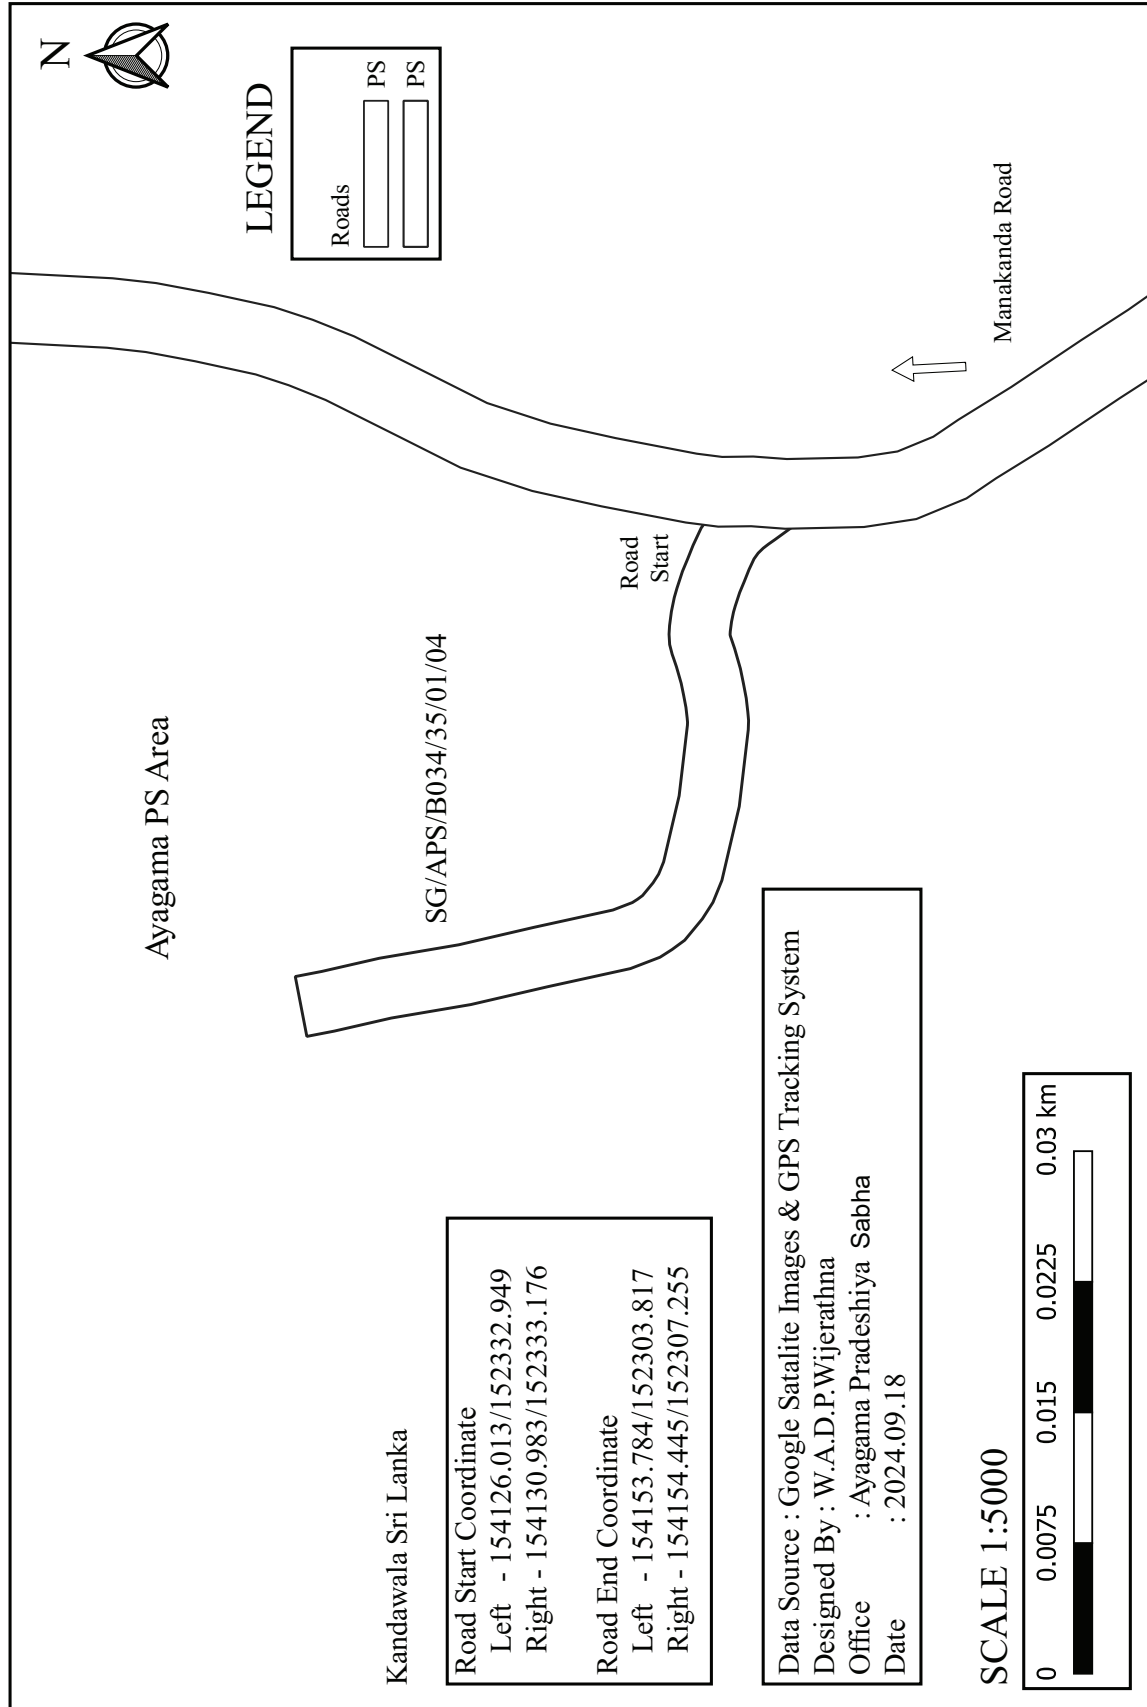


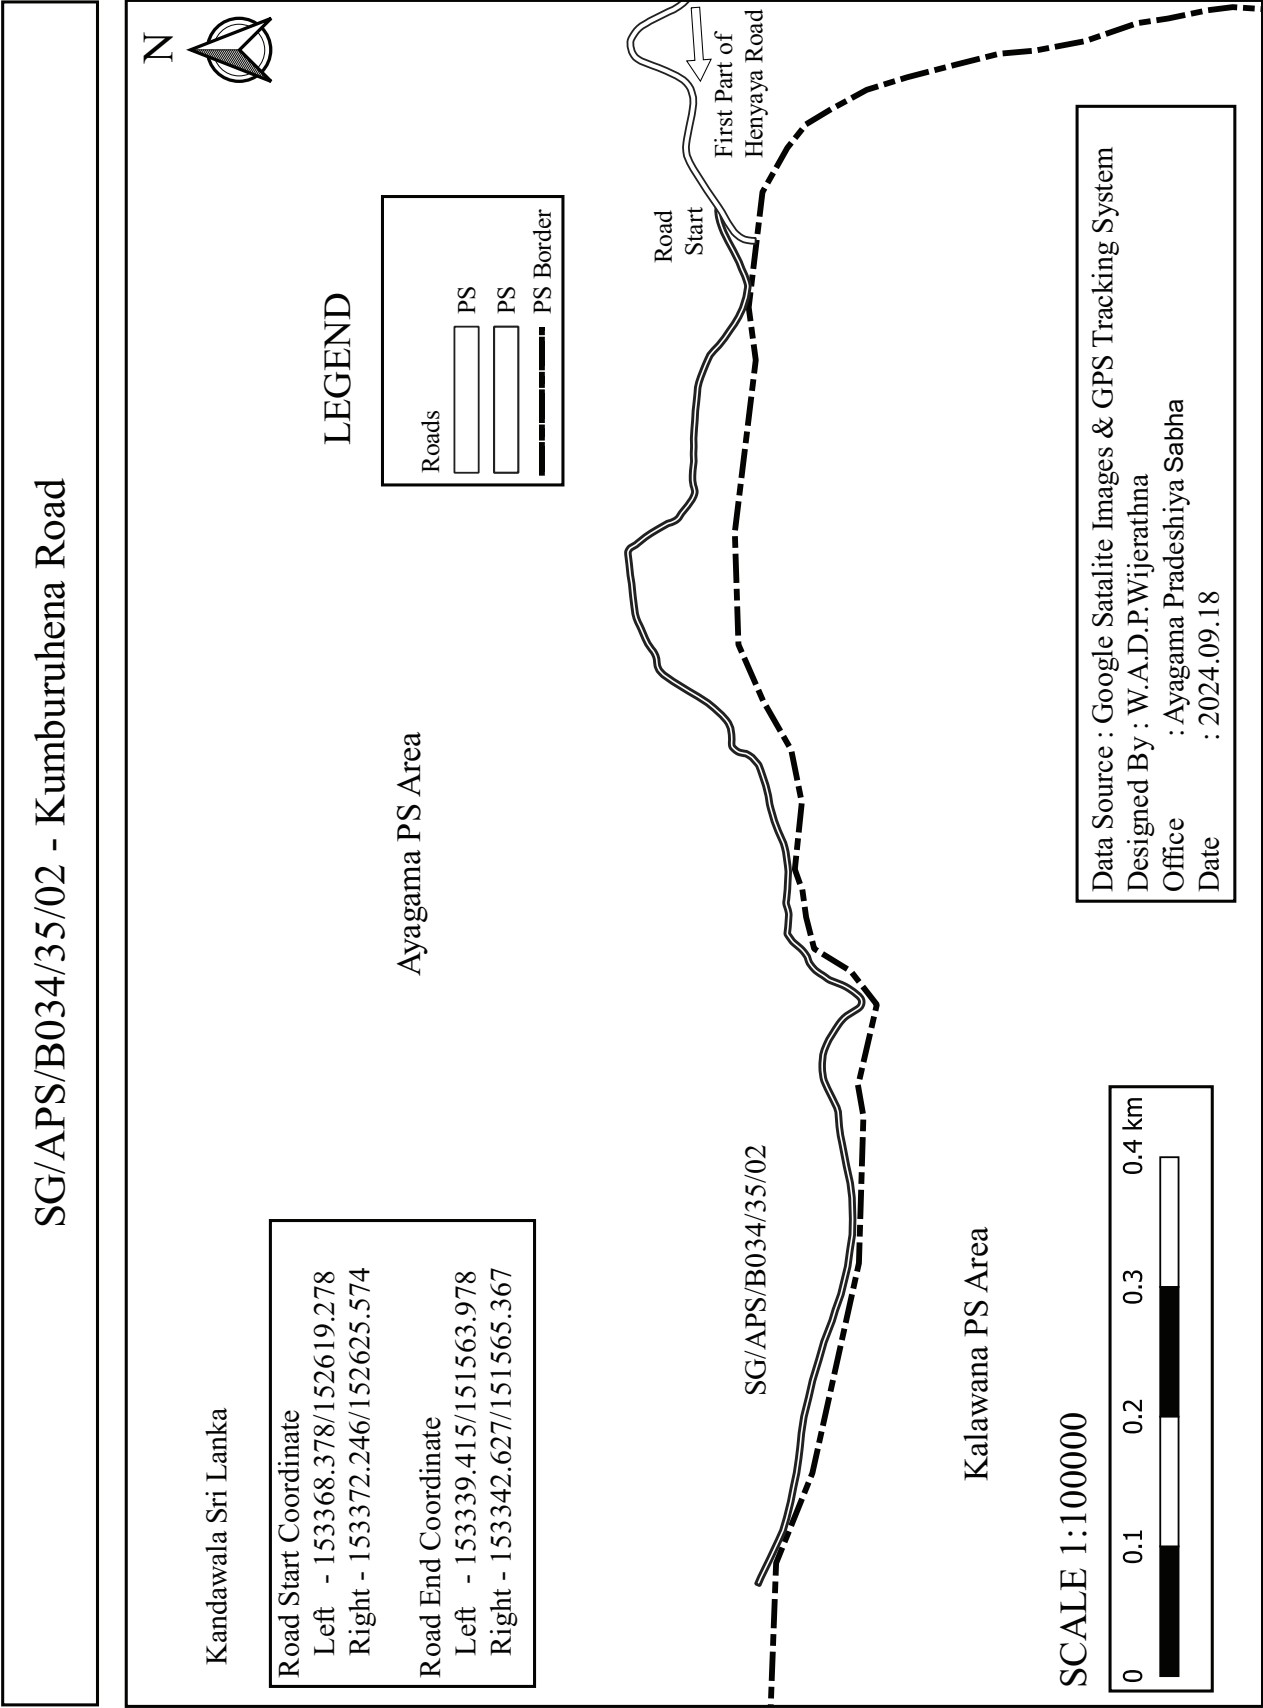



SG/APS/B034/36 - Kiwulahena Road

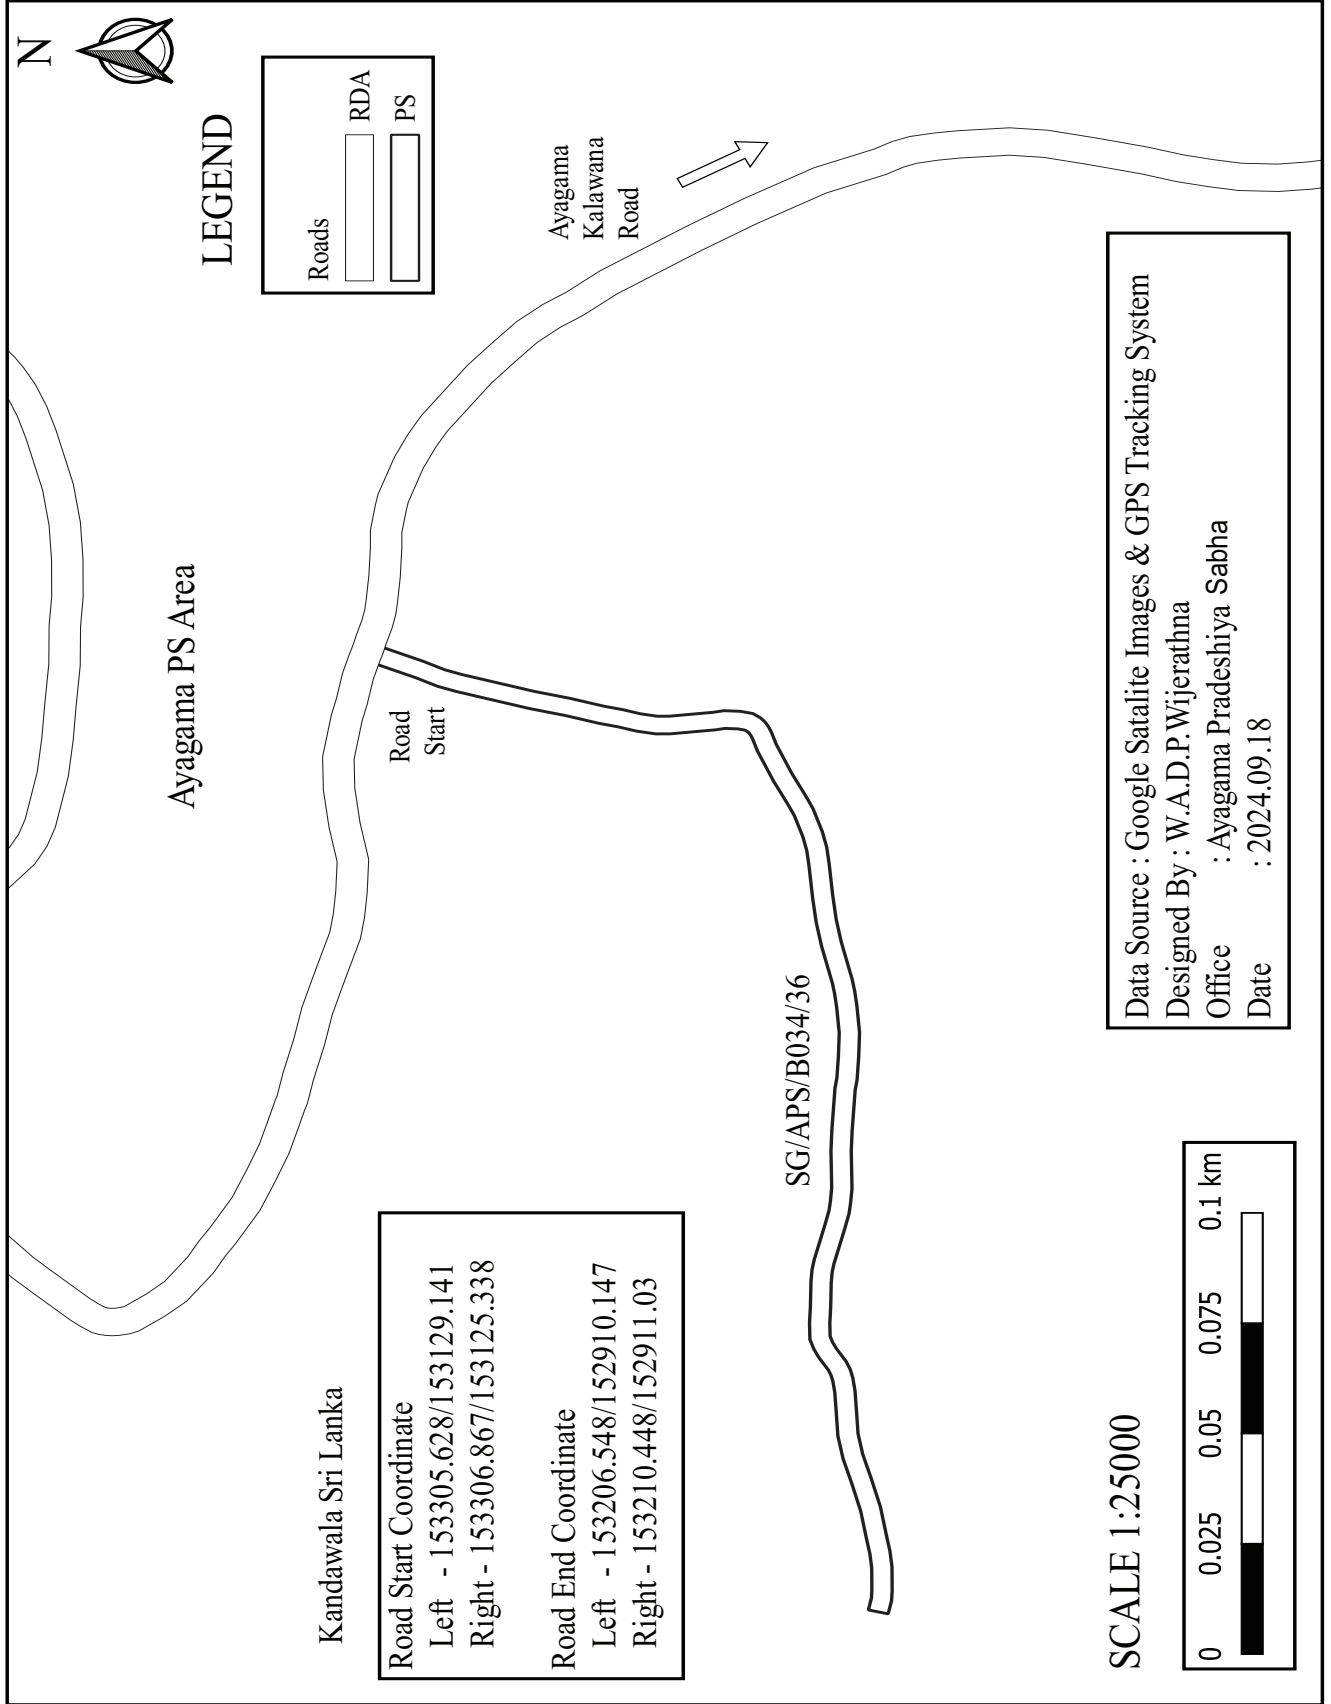


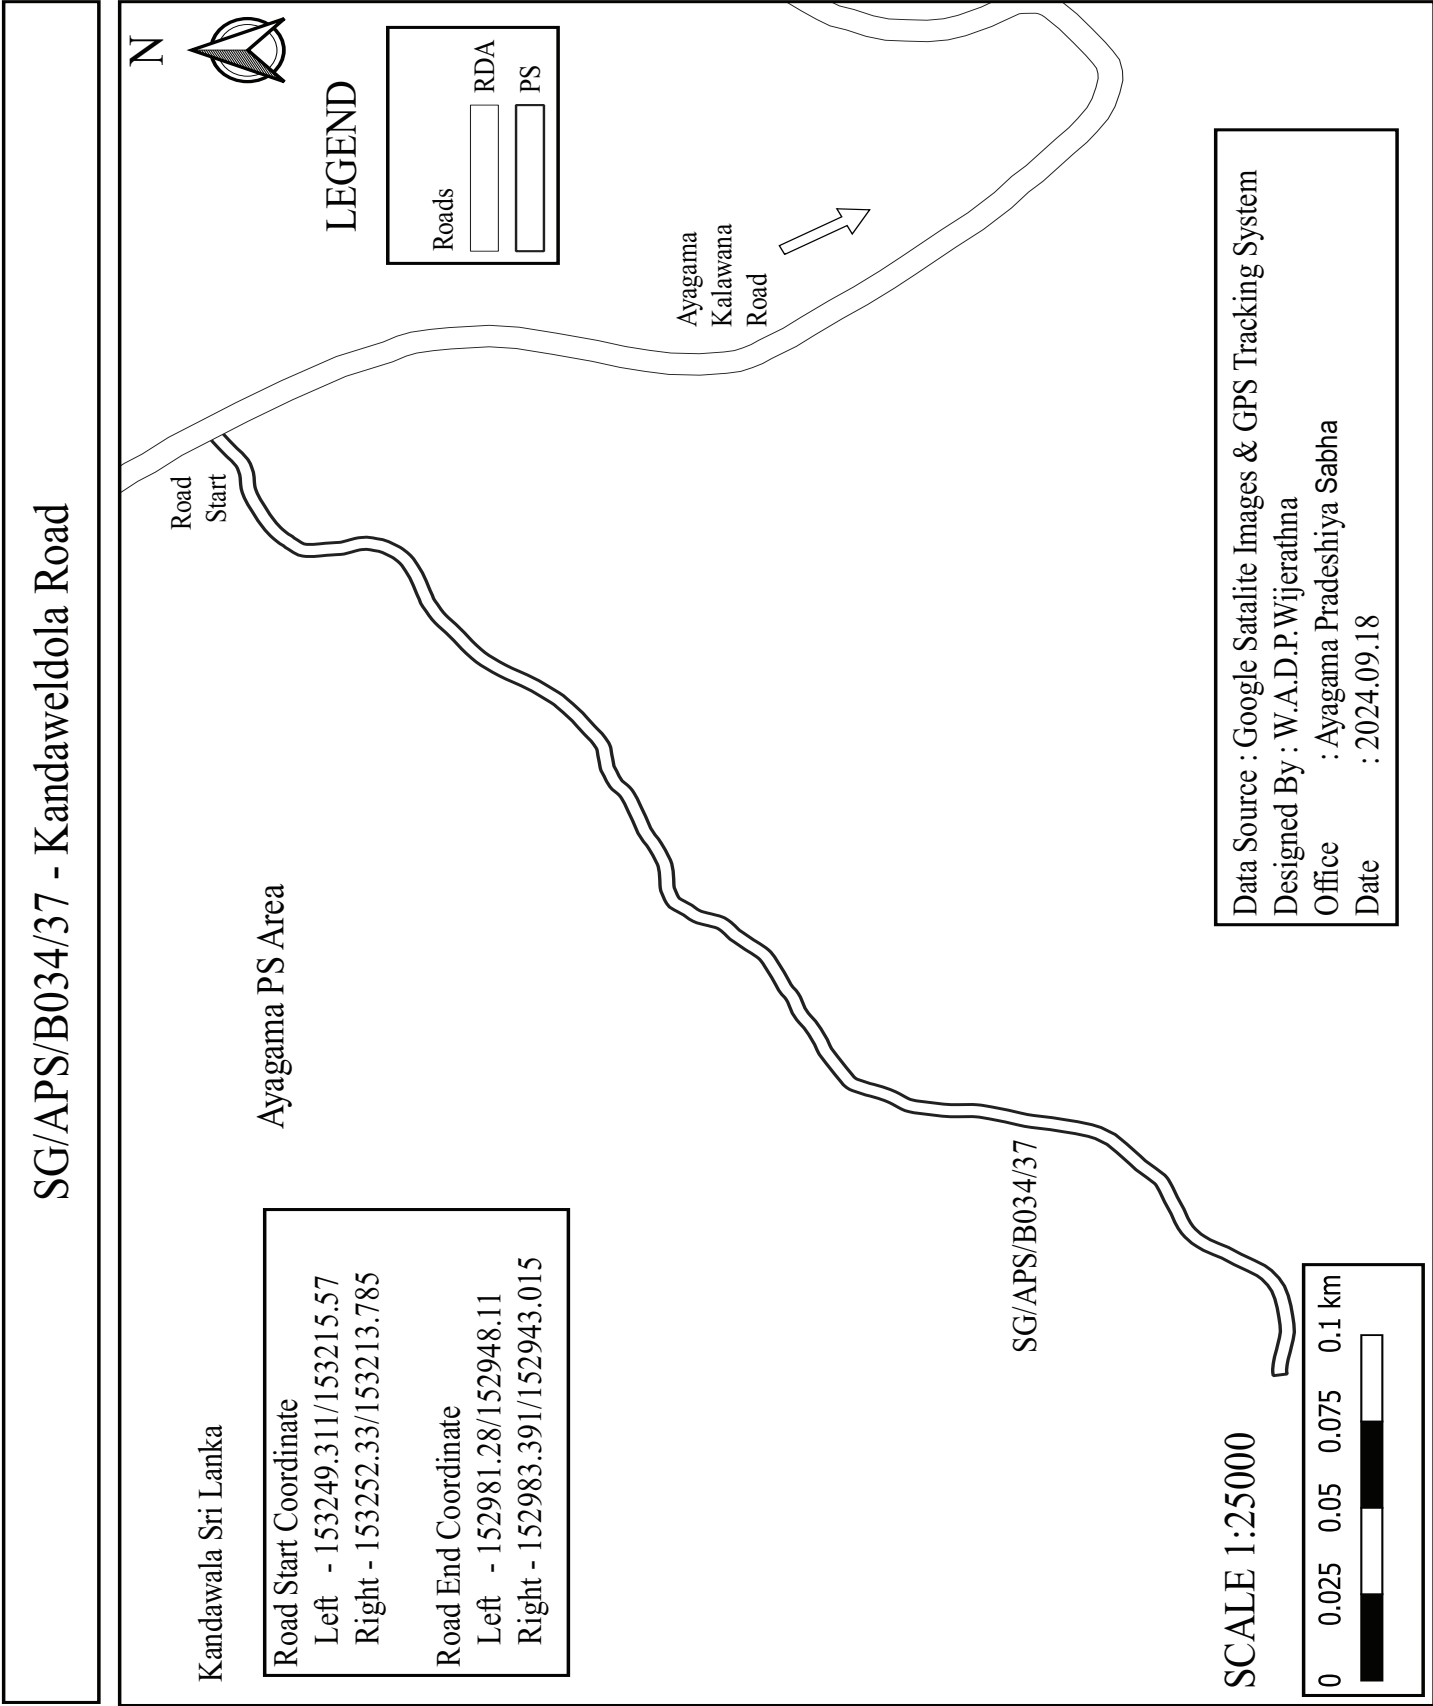


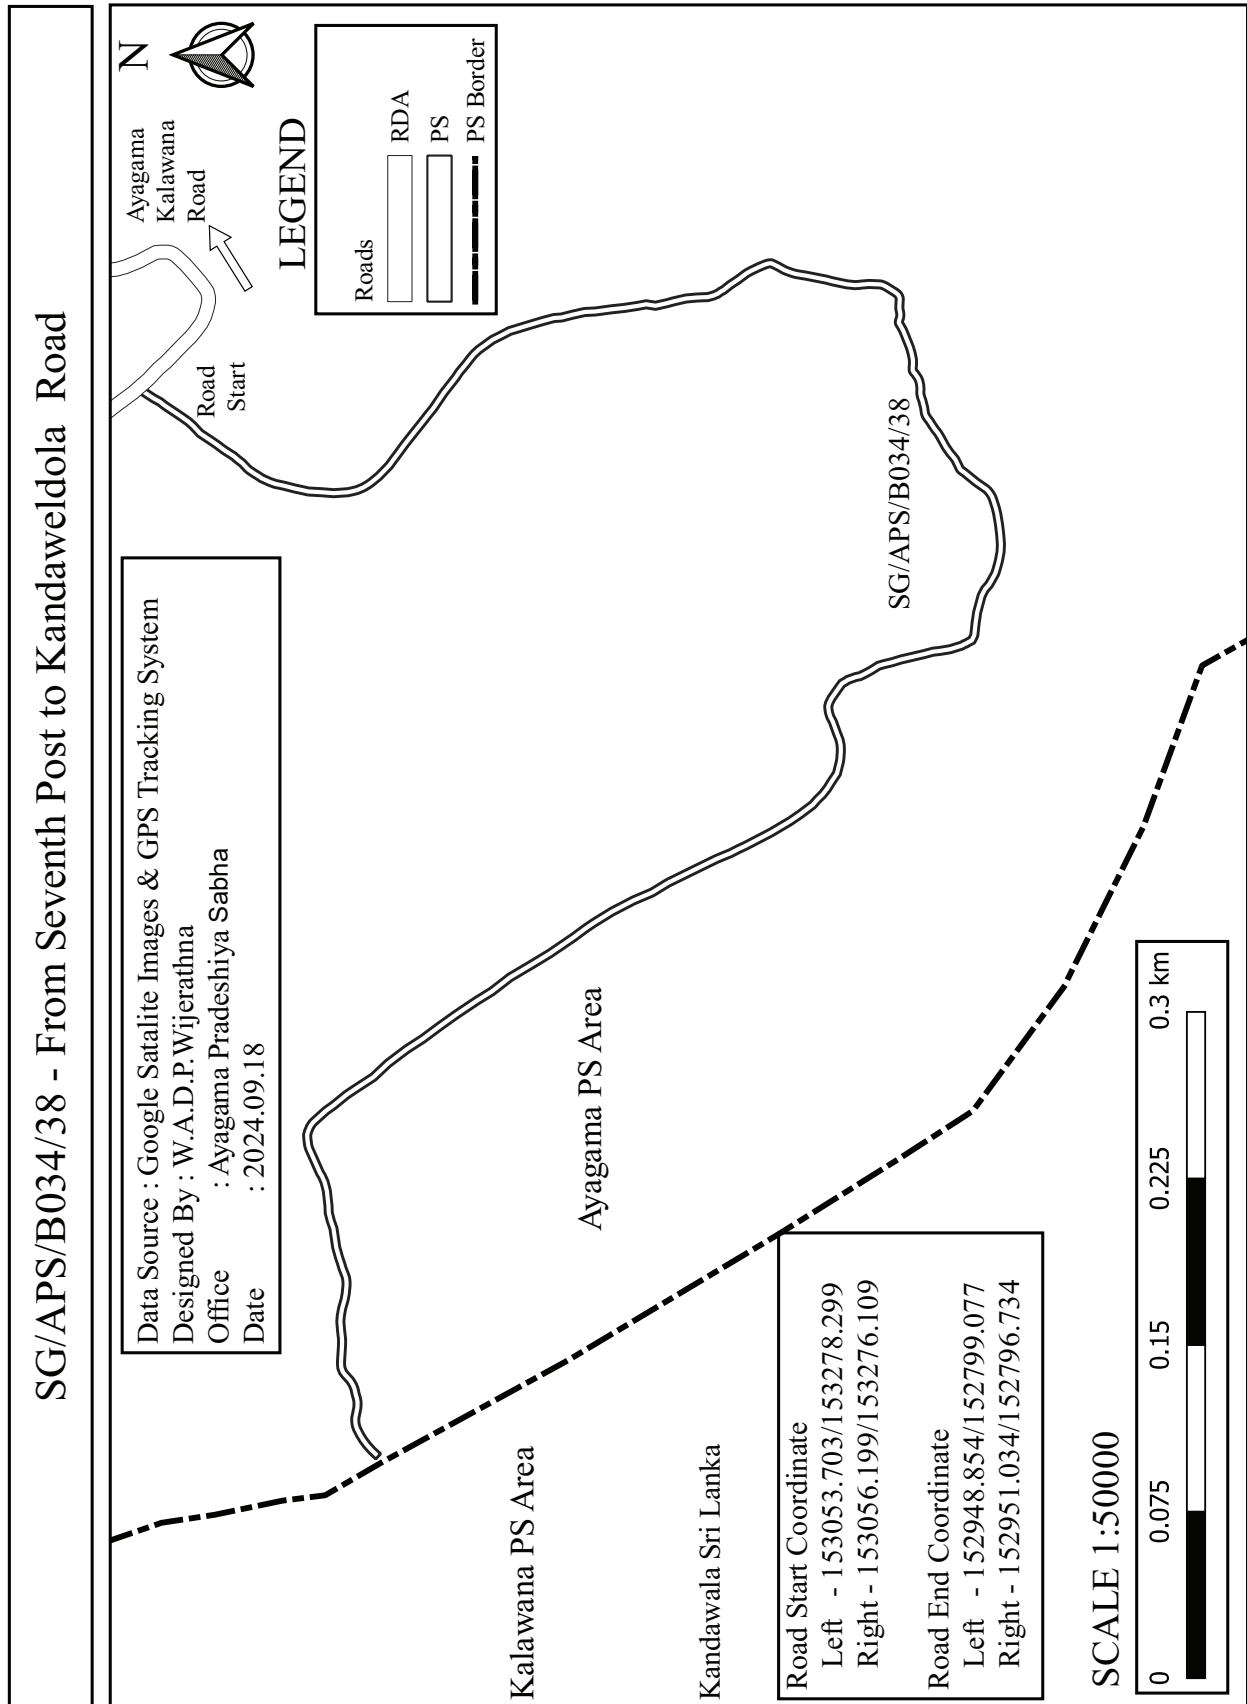


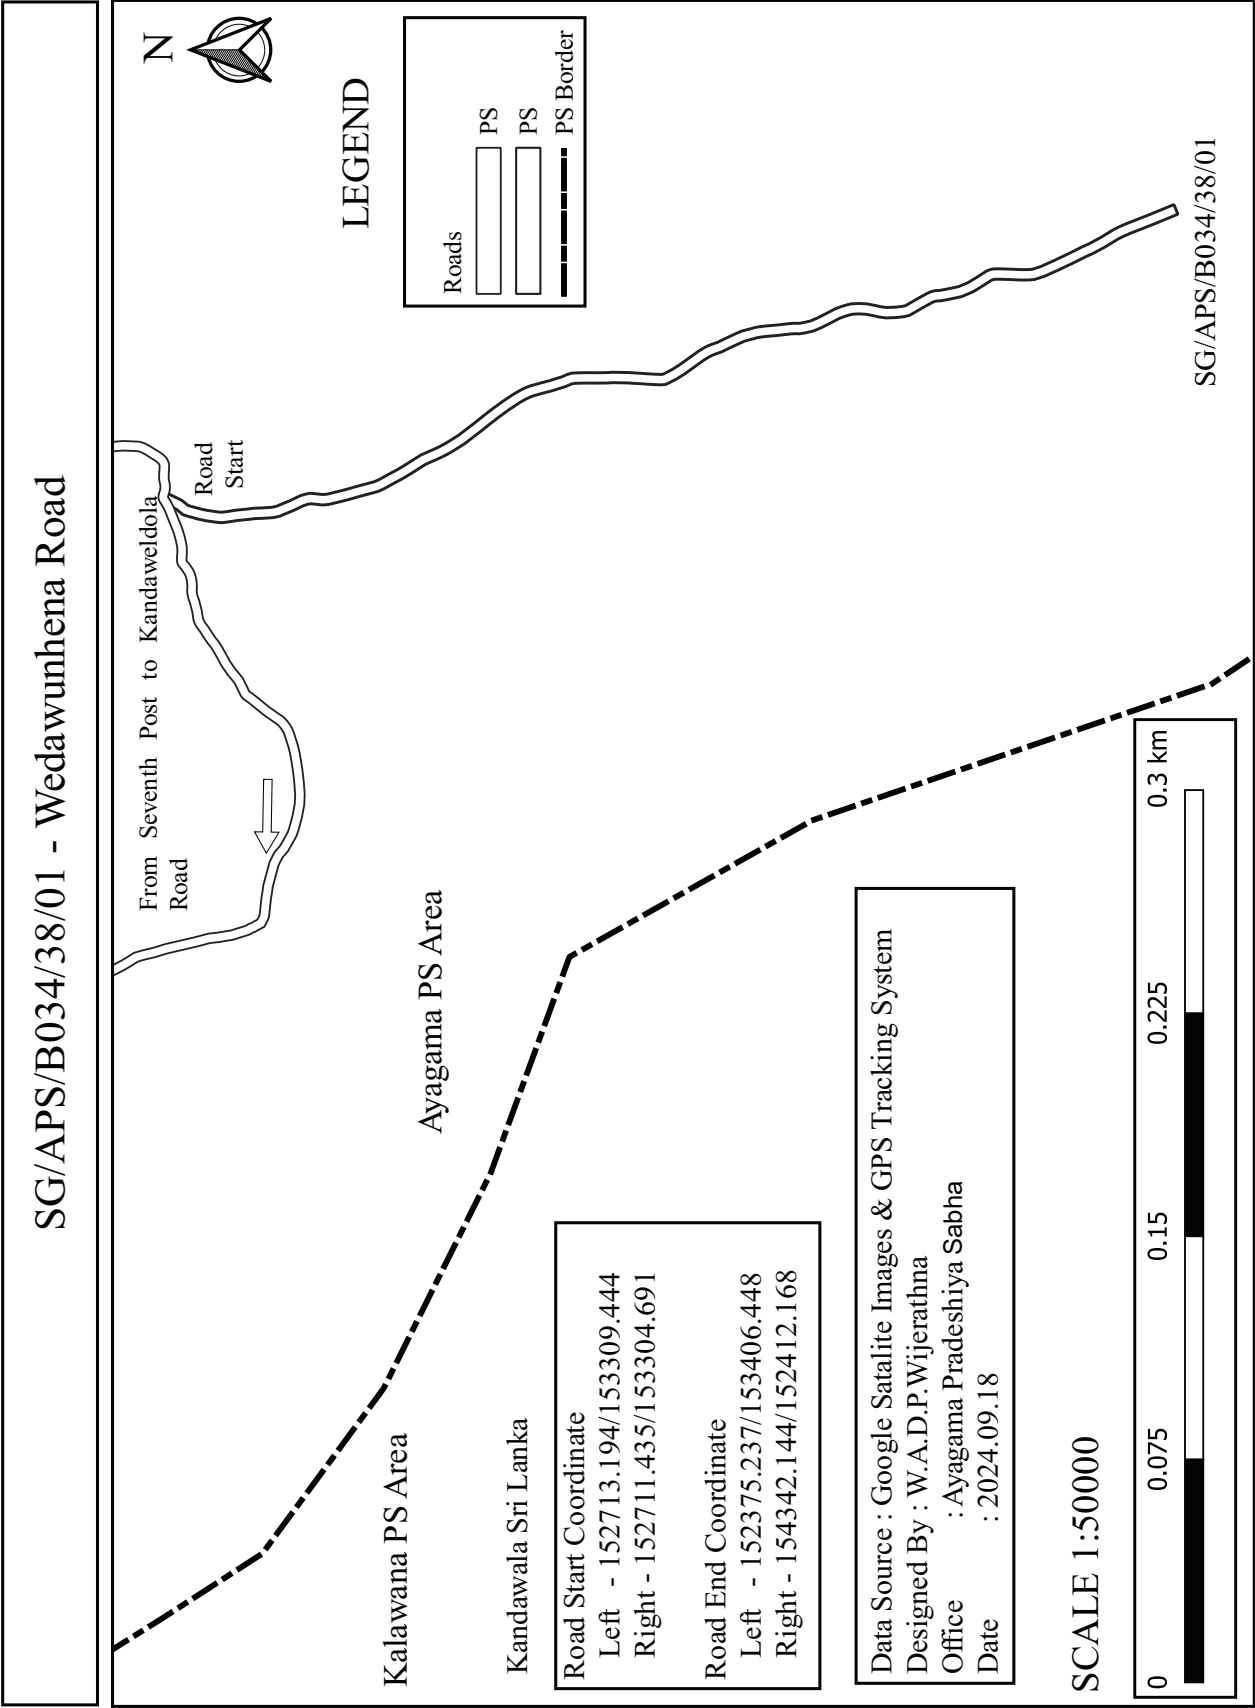


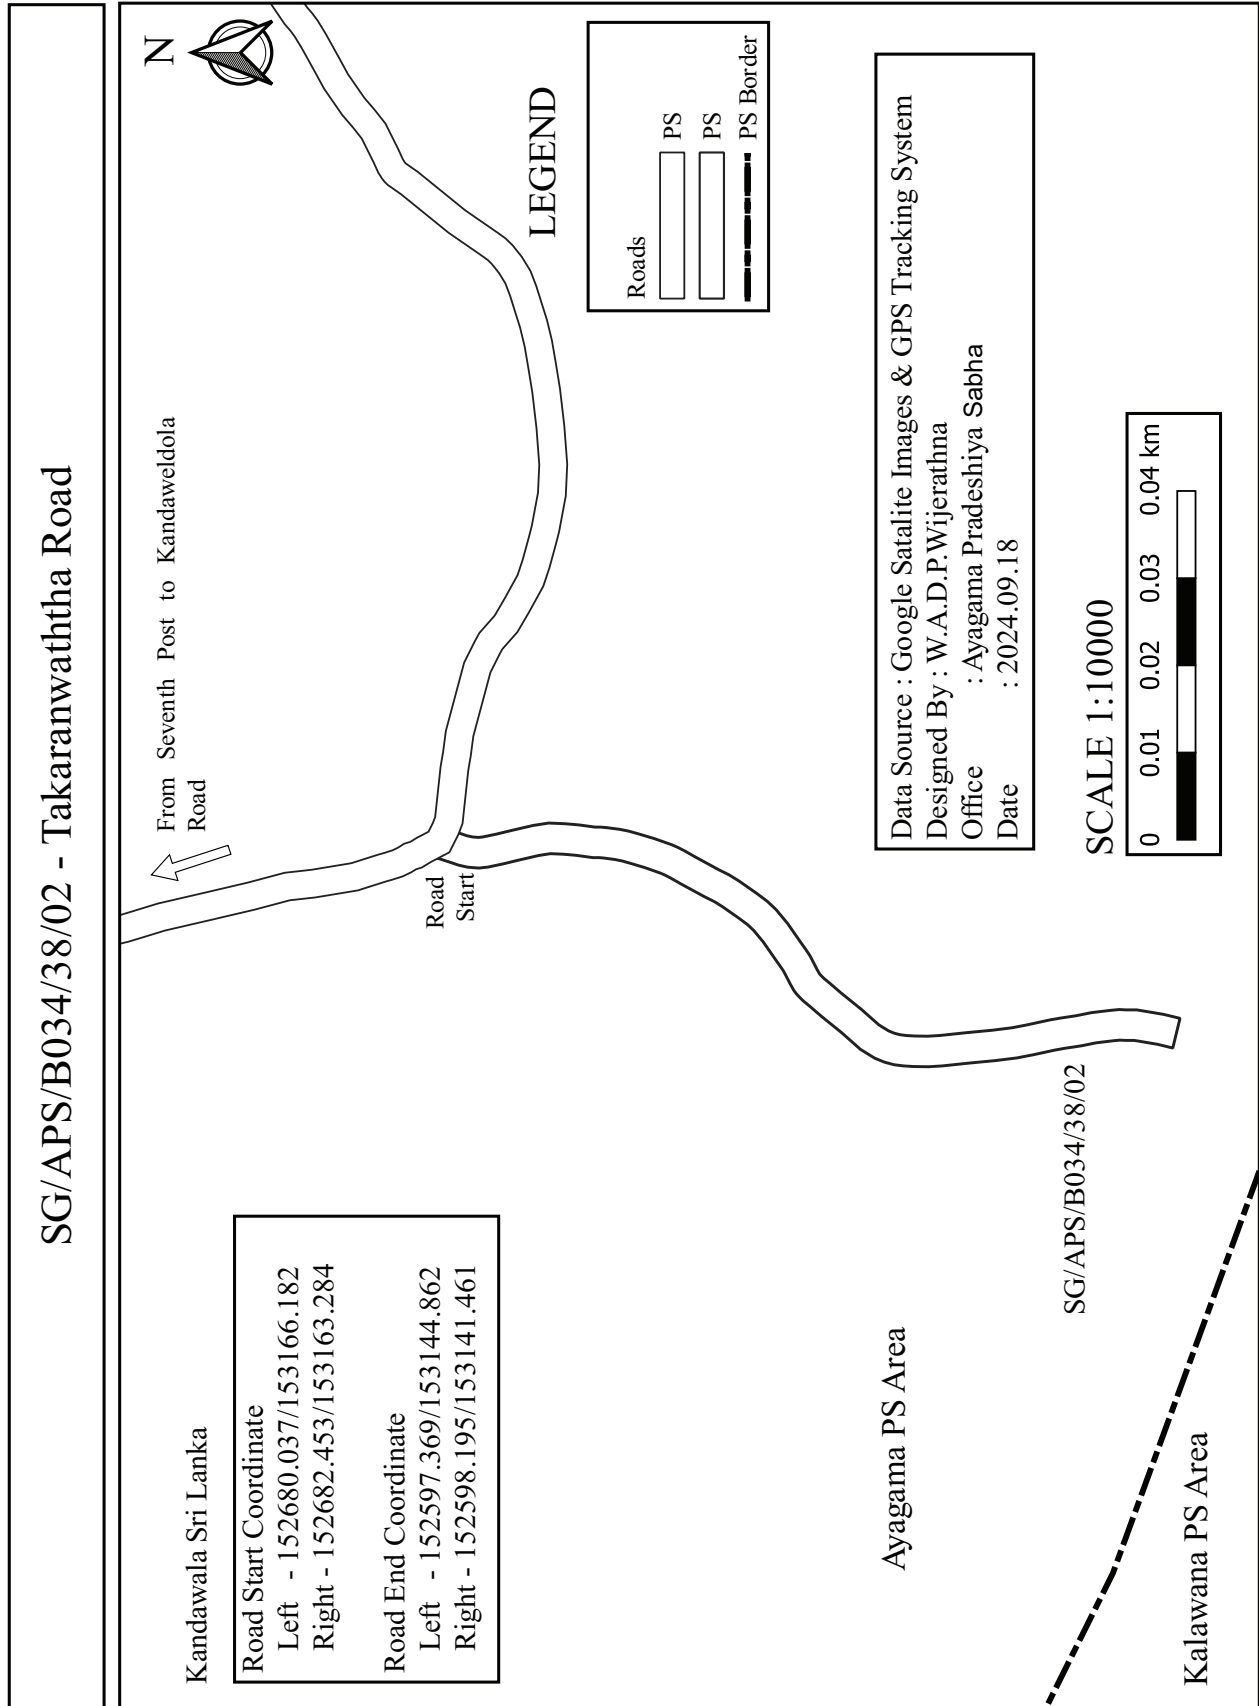


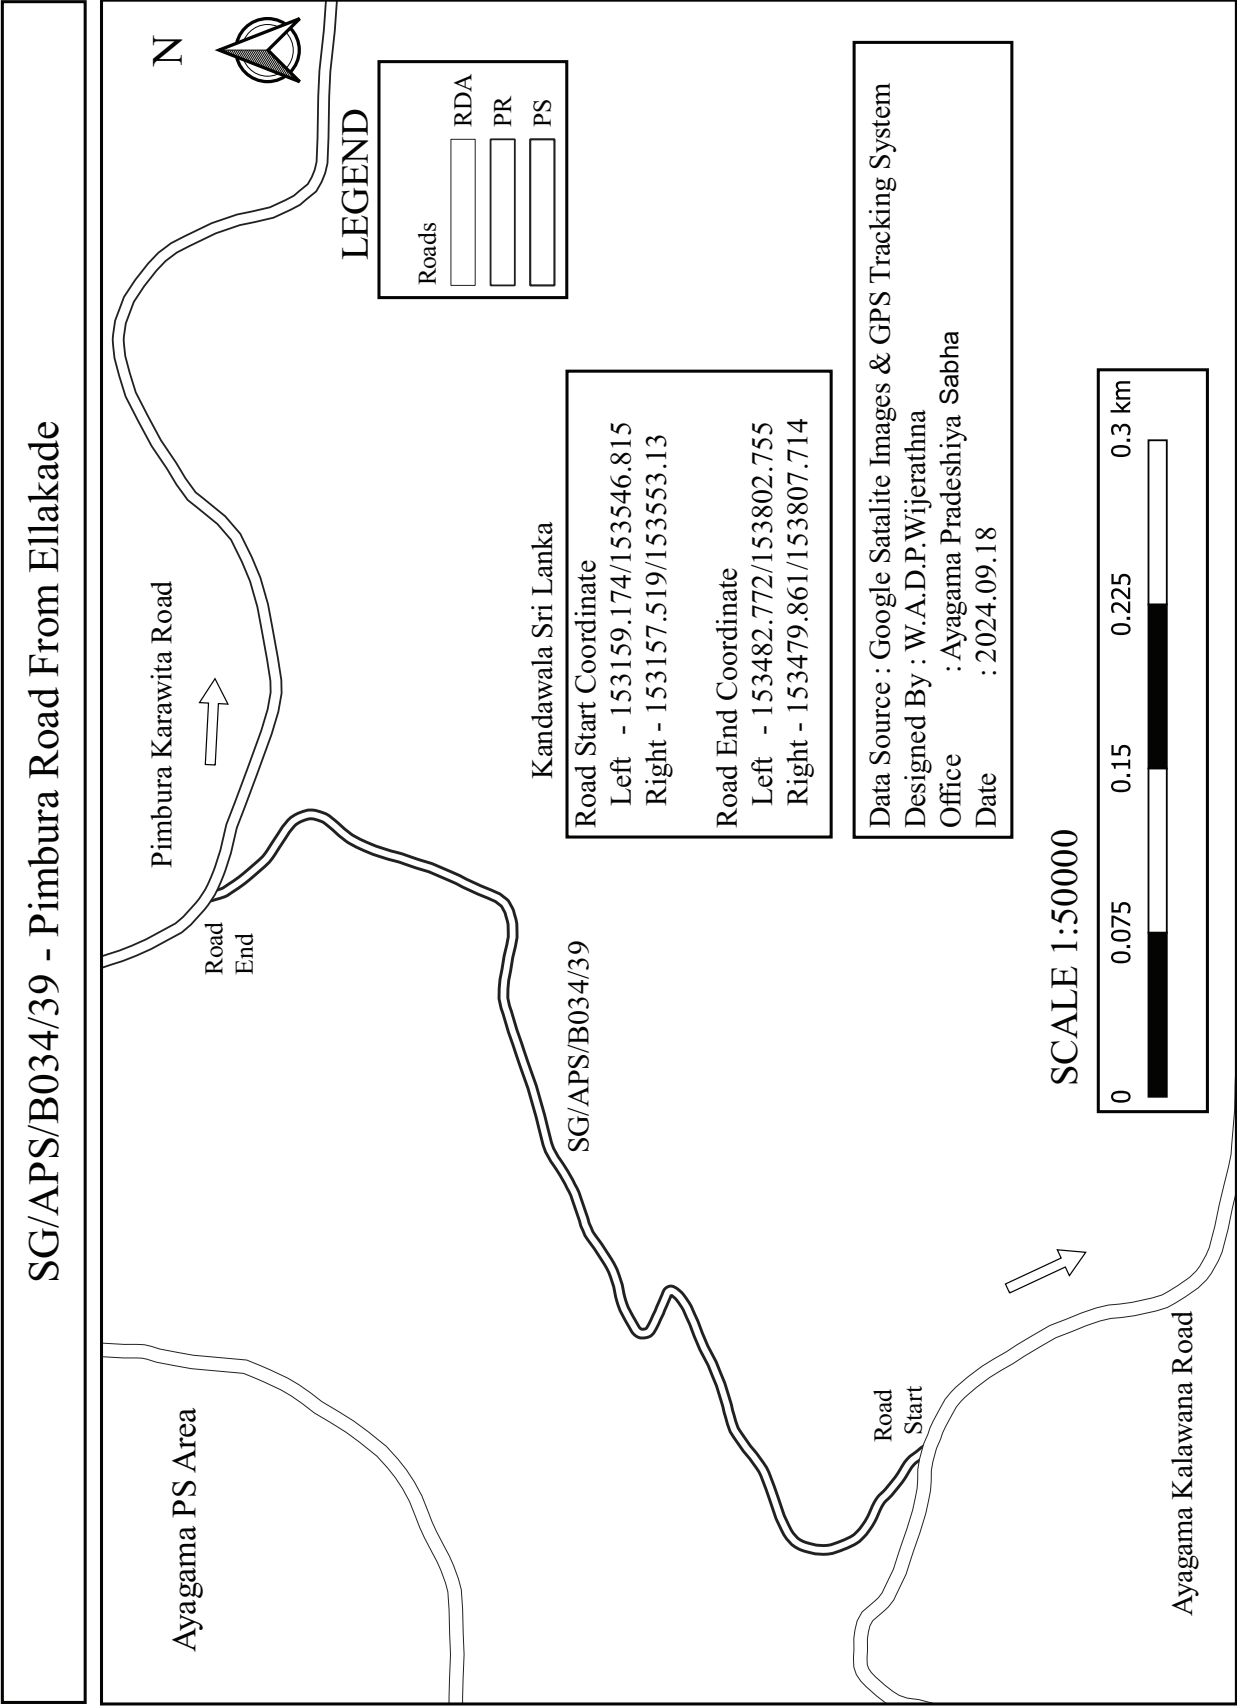


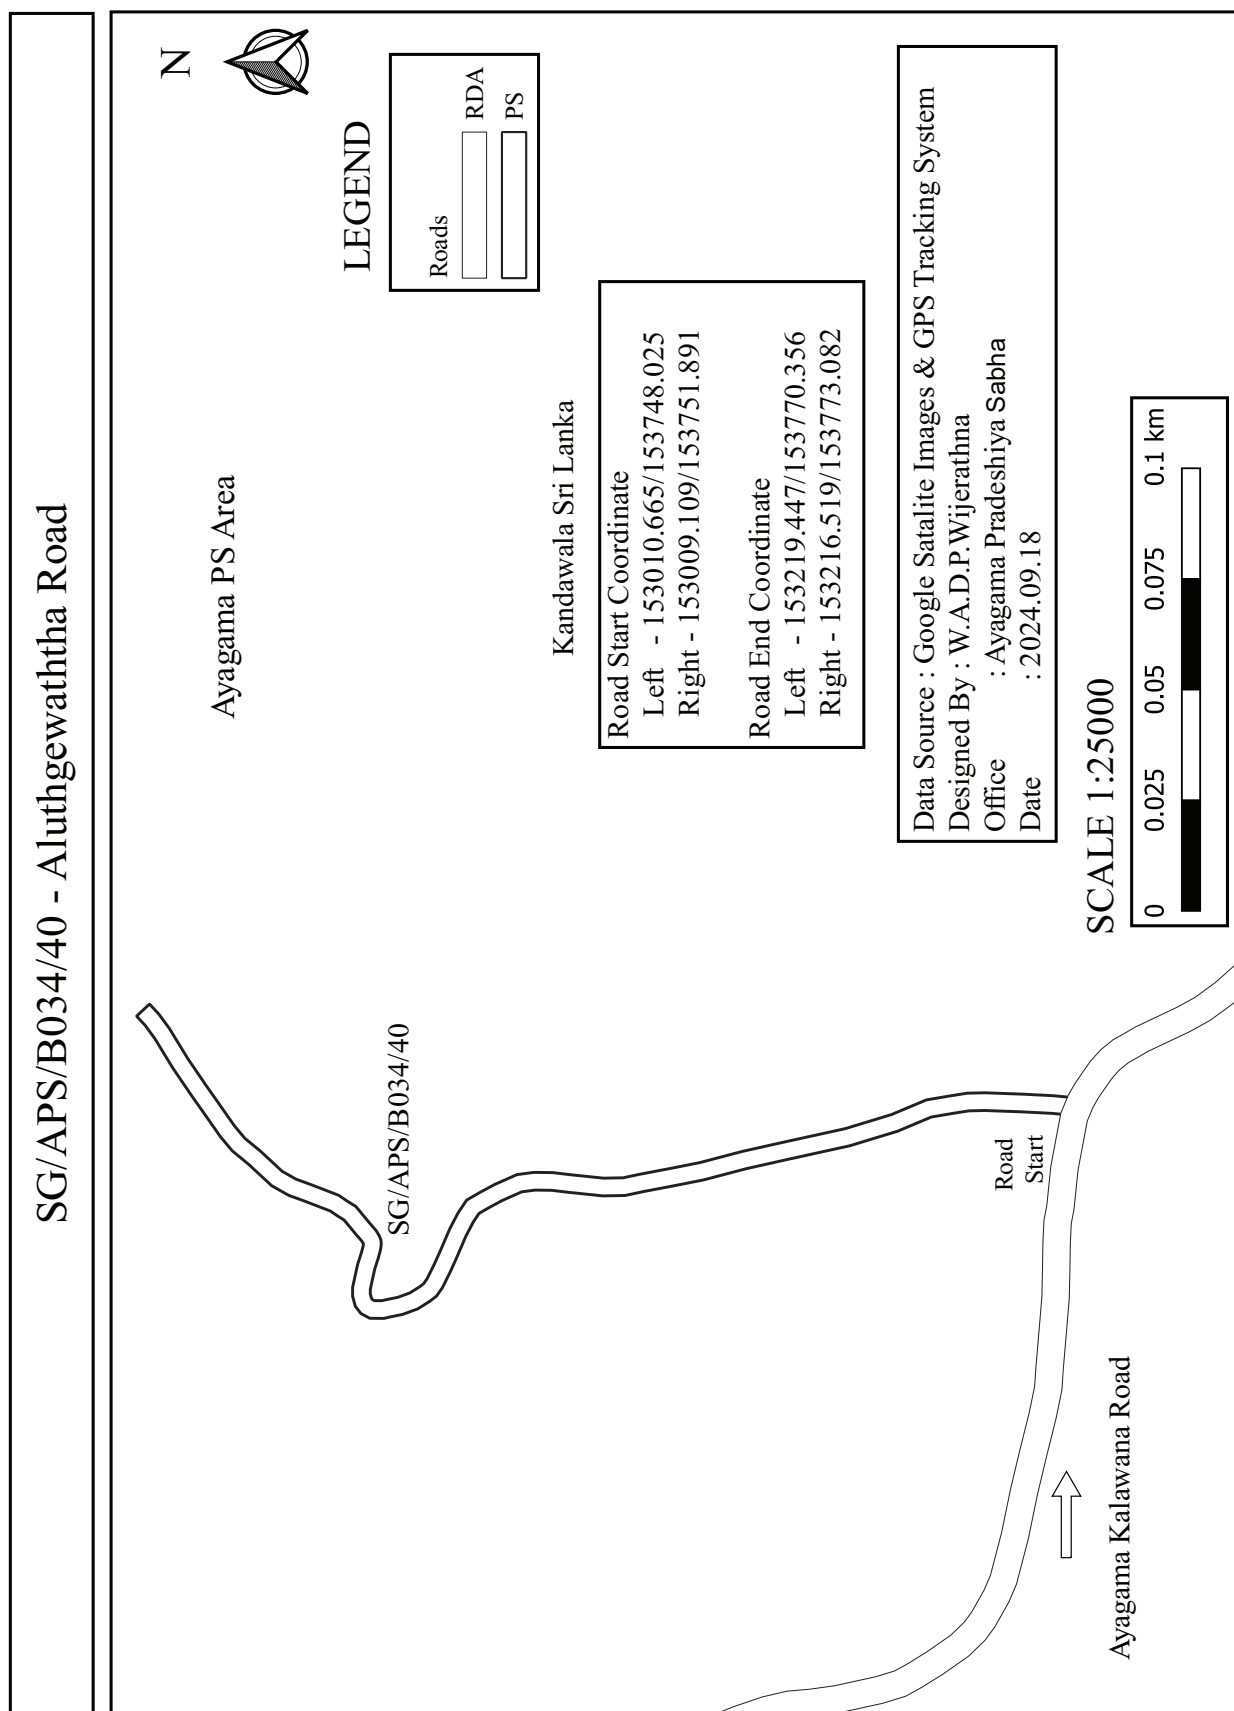


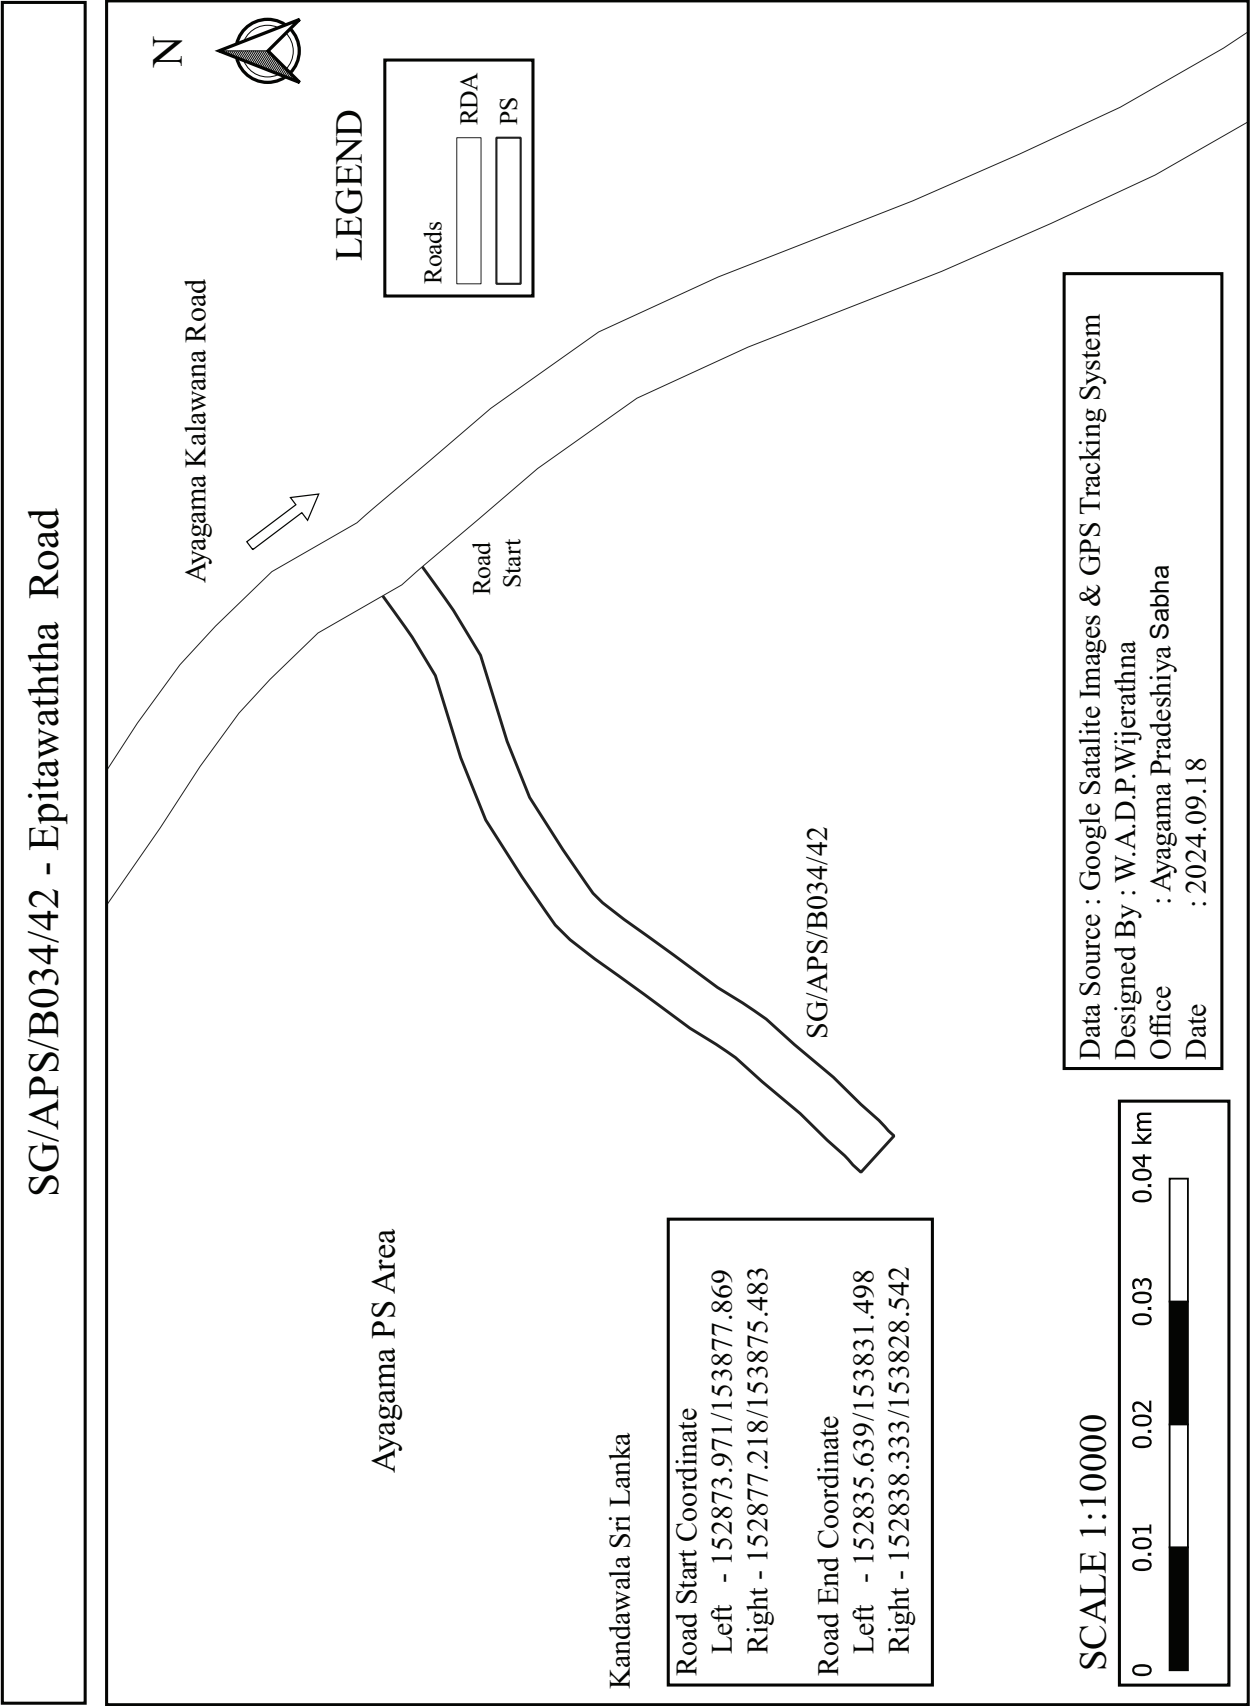

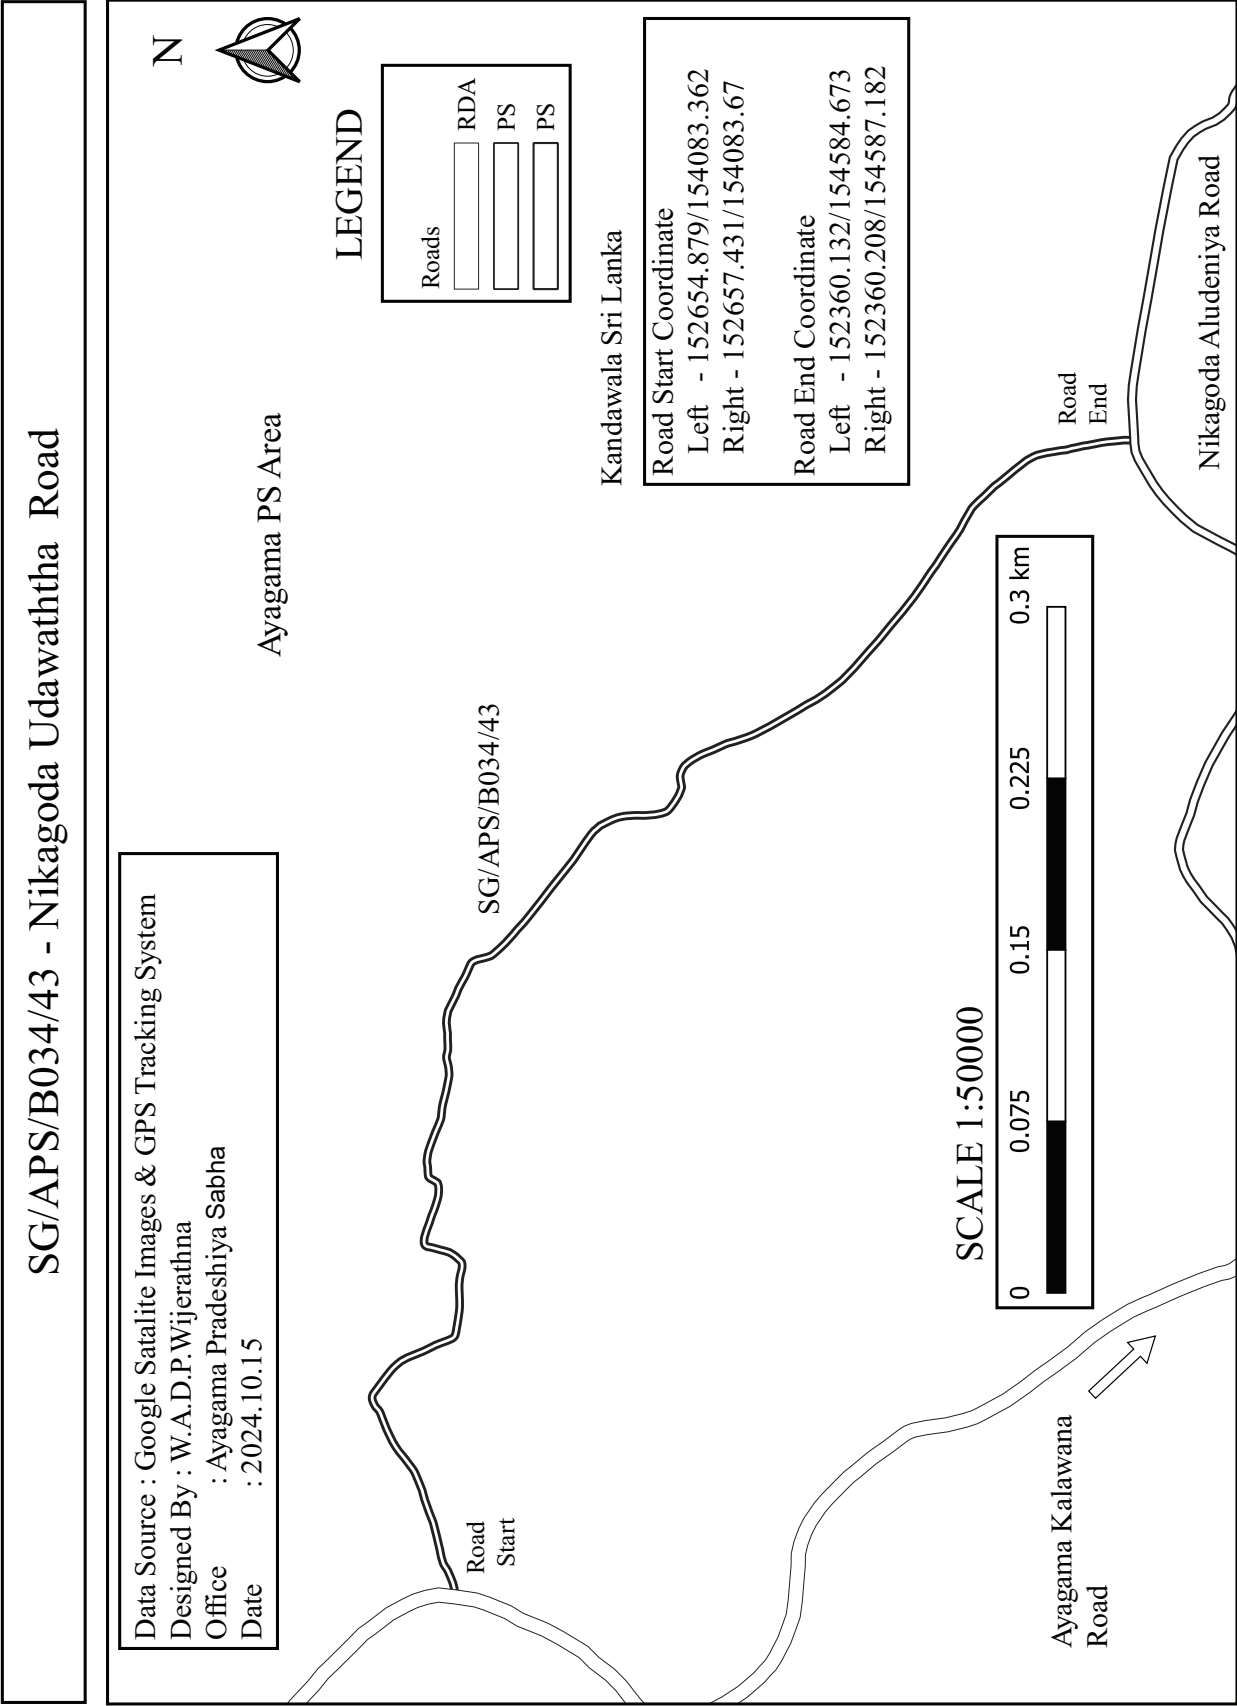

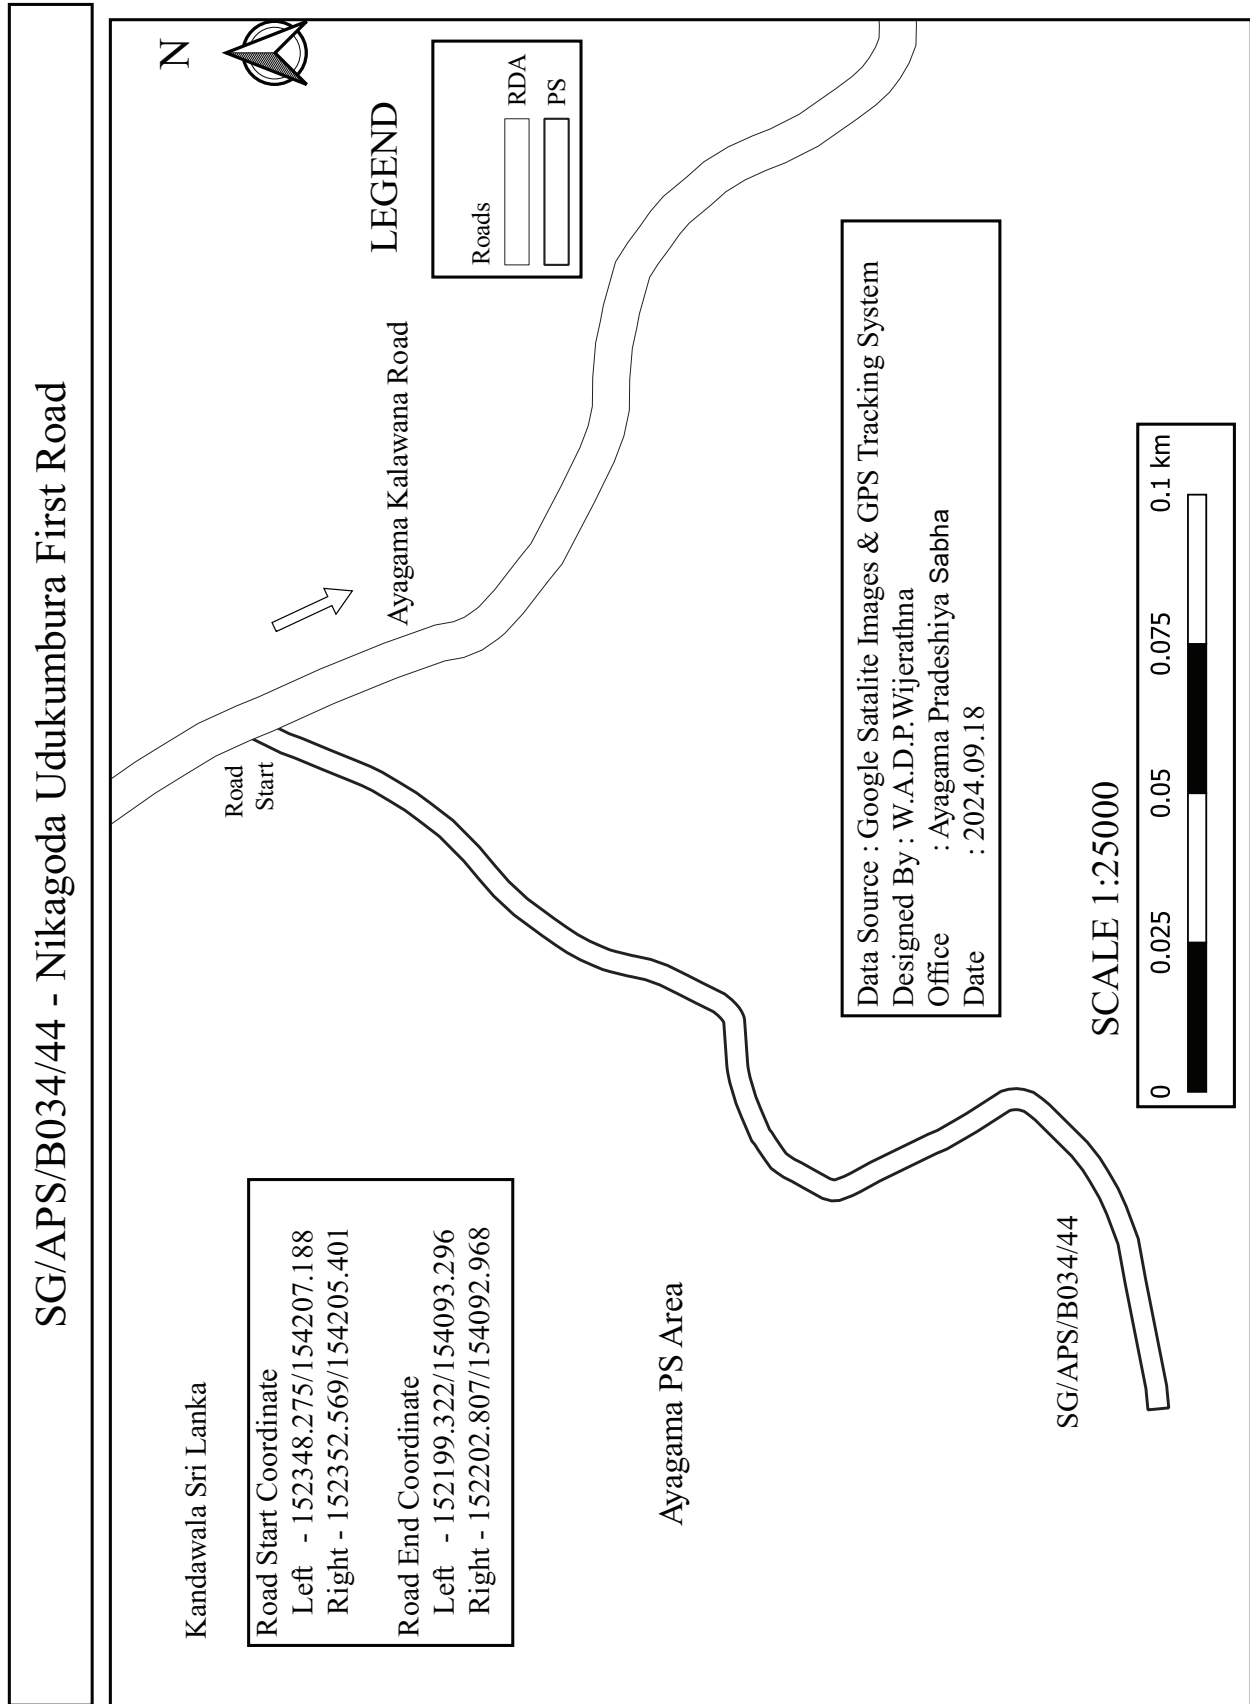

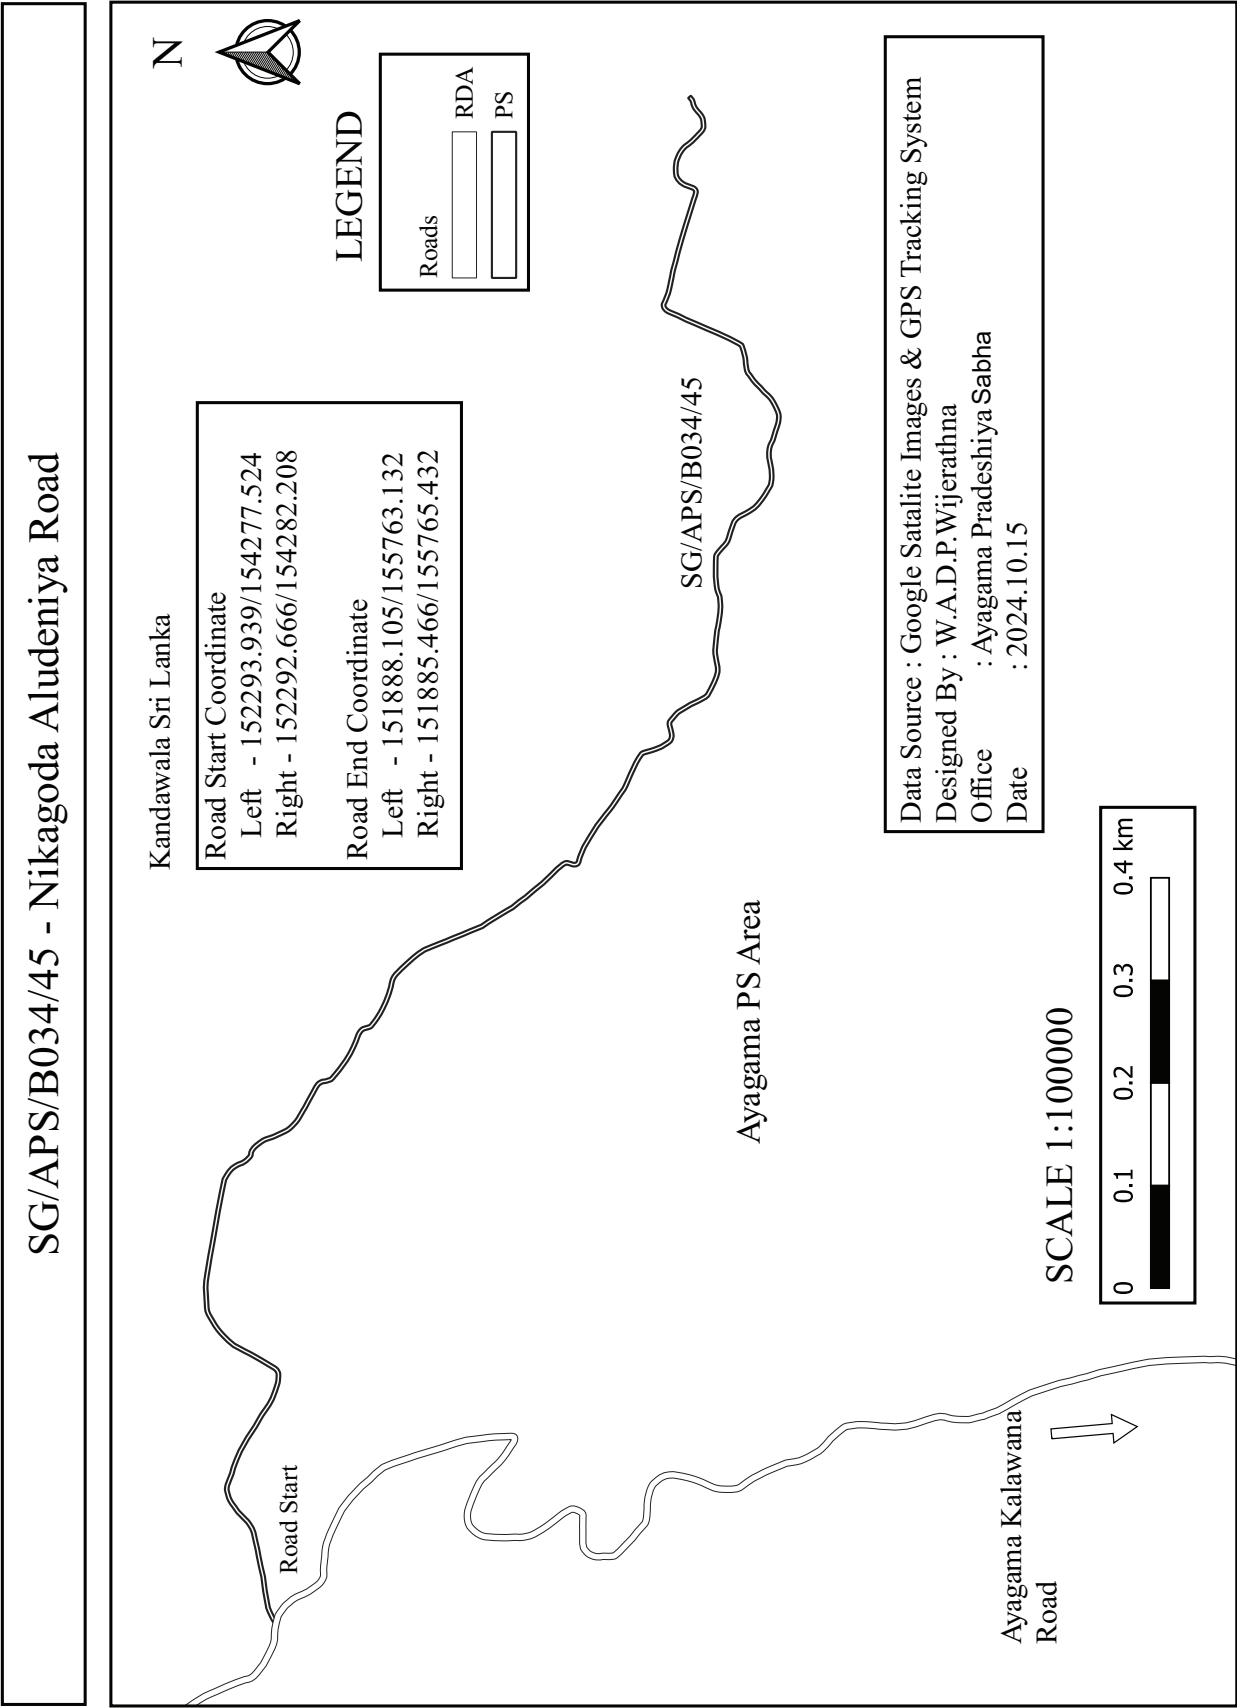


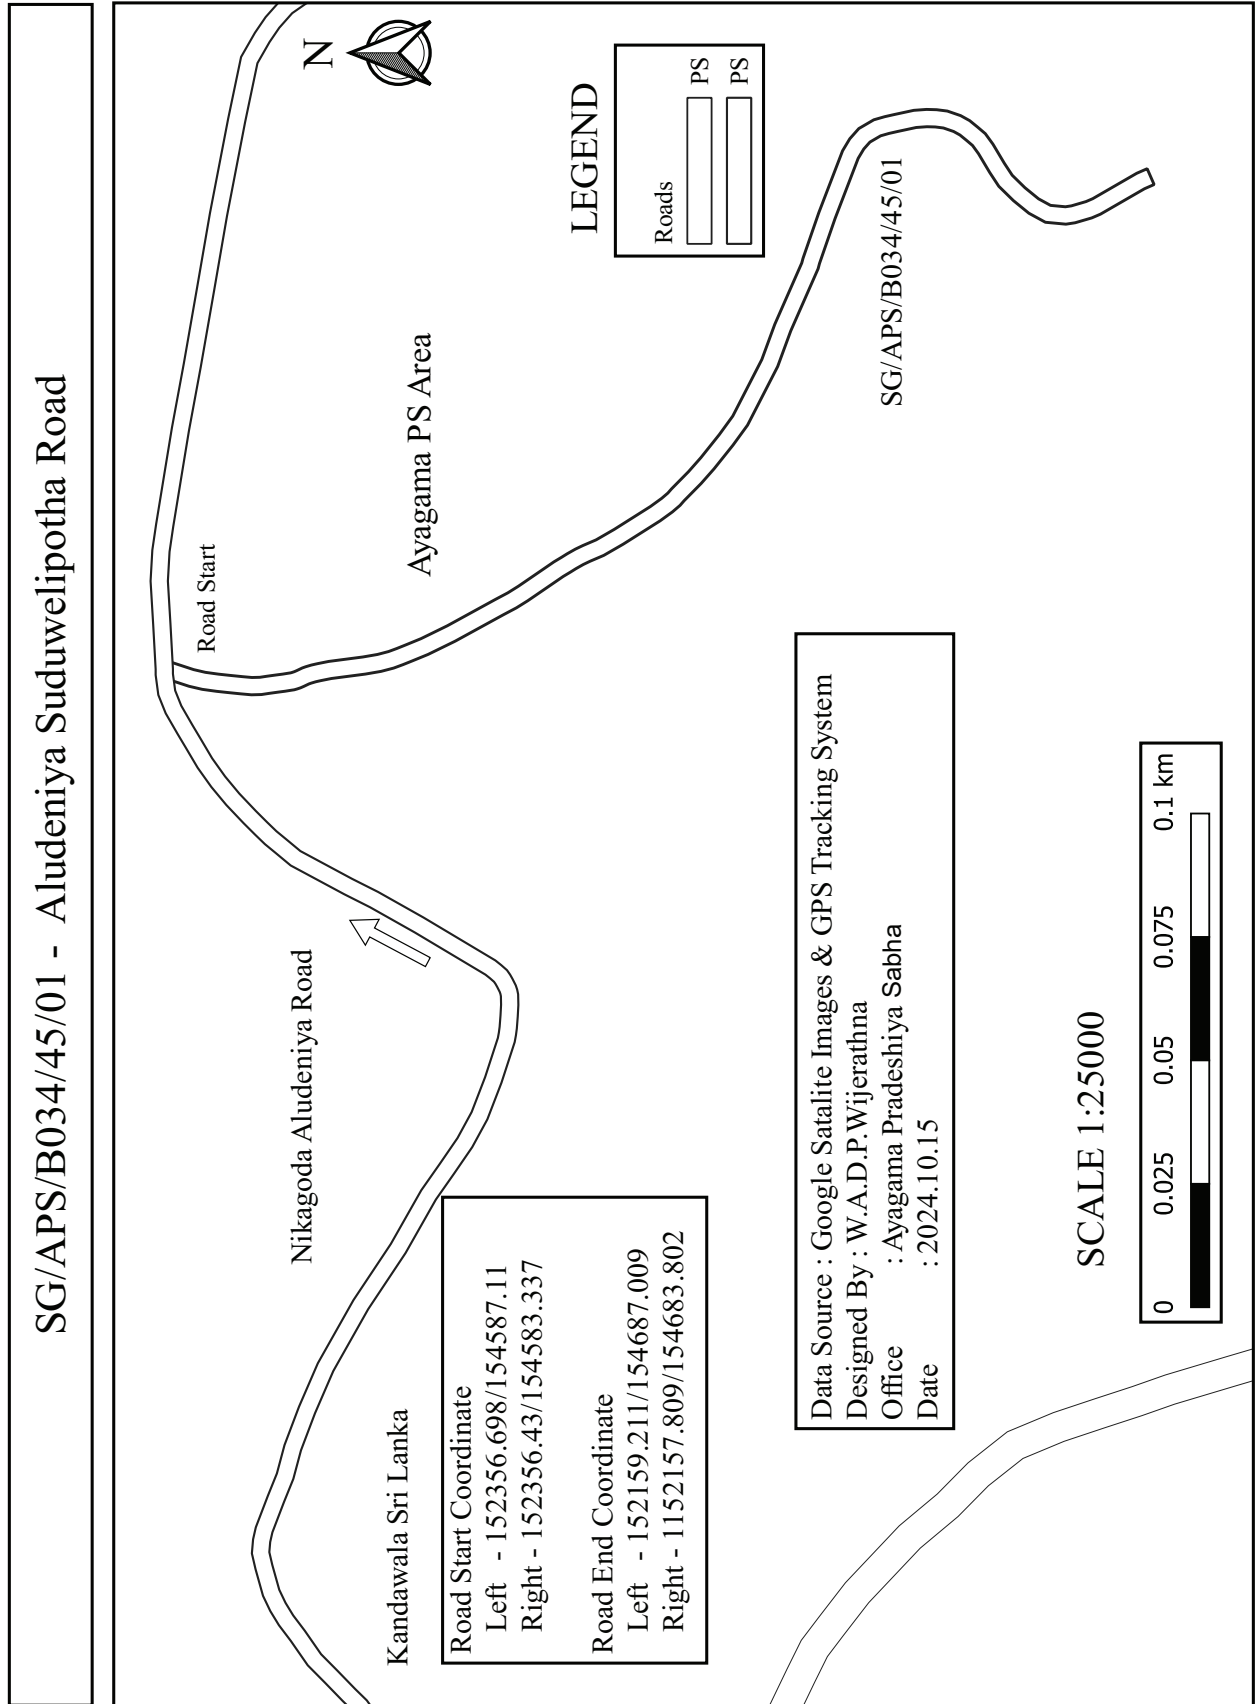



SCALE 1:25000

0 0.025 0.05 0.075 0.1 km

Data Source : Google Satalite Images & GPS Tracking System
Designed By : W.A.D.P.Wijerathna
Office : Ayagama Pradeshiya Sabha
Date : 2024.10.15

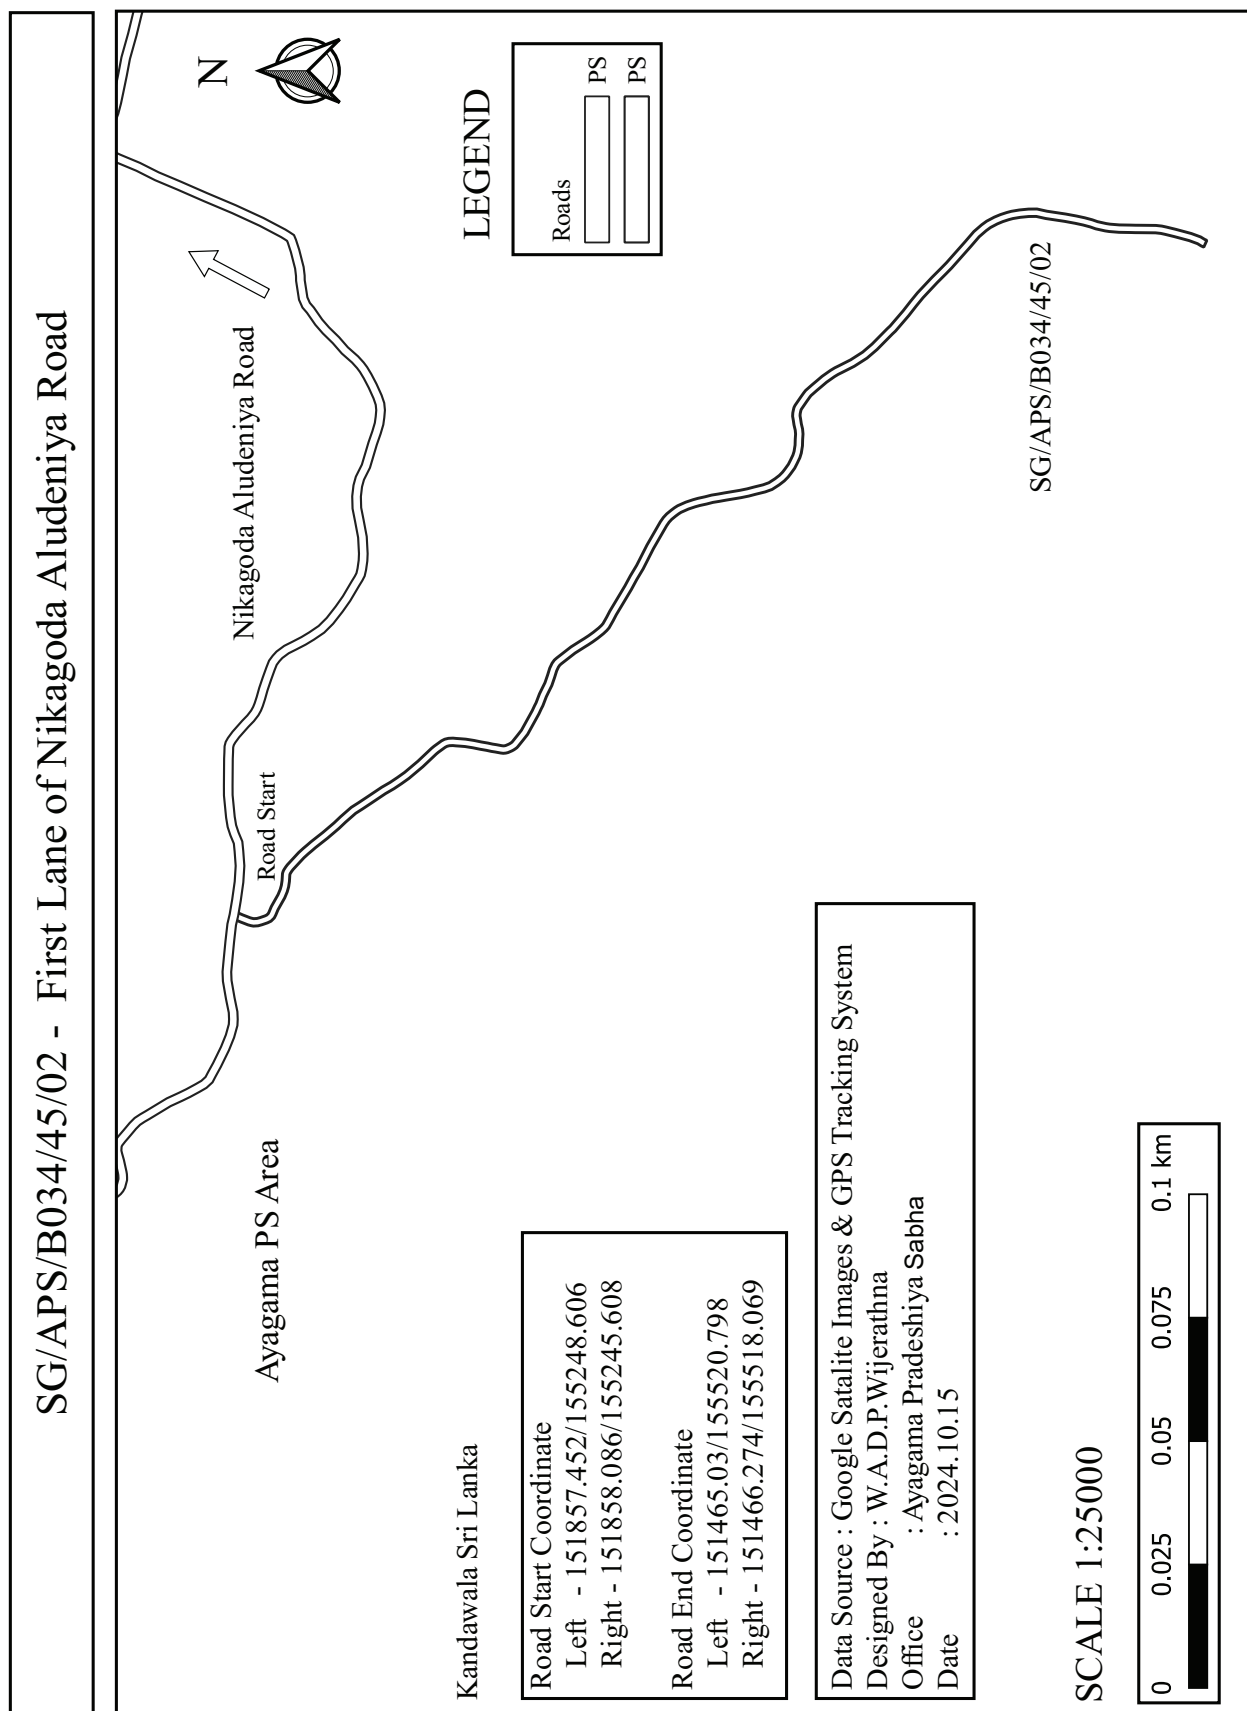

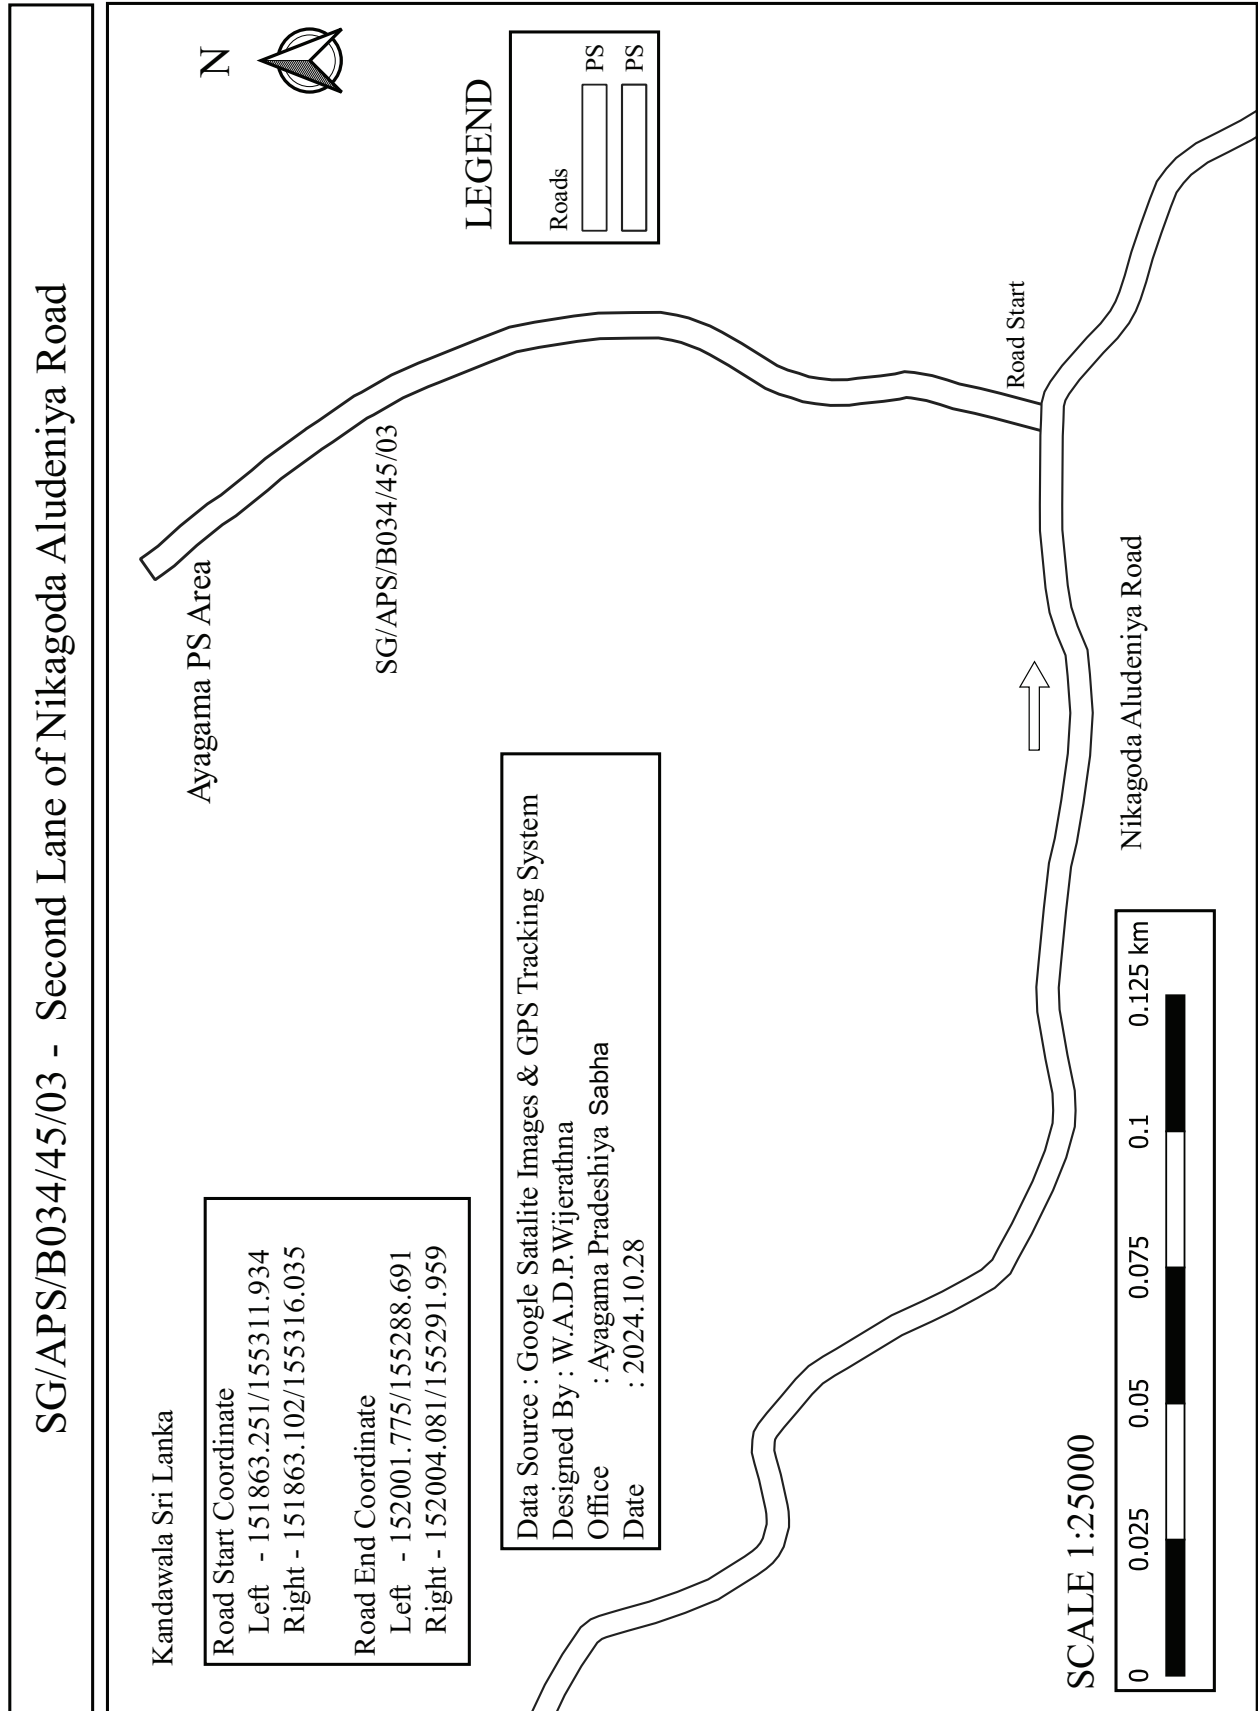

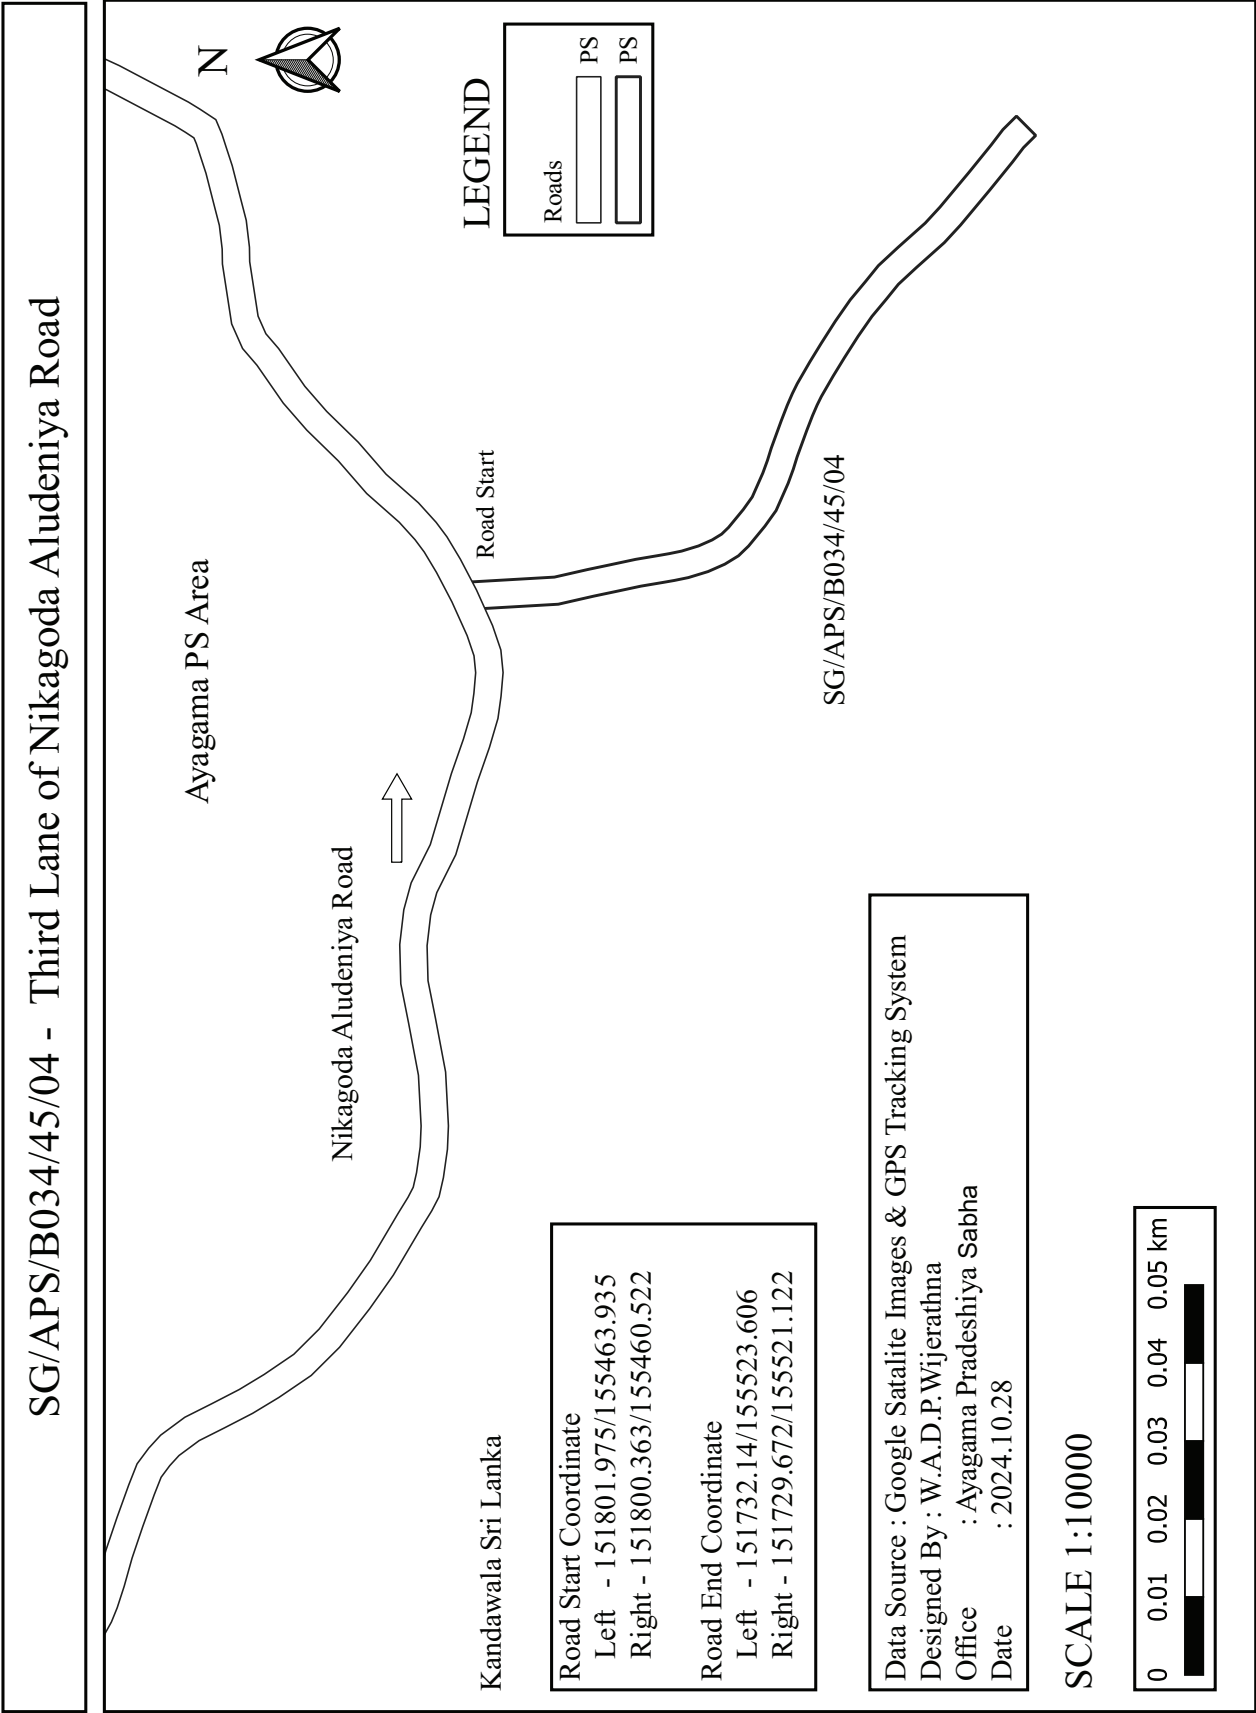

SG/APS/B034/45/05 - Fourth Lane of Nikagoda Aludeniya Road

Kandawala Sri Lanka

Road Start Coordinate

Left - 151836.428/155524.305

Right - 151834.142/155521.646

Road End Coordinate

Left - 151834.407/155586.377

Right - 151835.461/155589.714


Data Source : Google Satalite Images & GPS Tracking System

Designed By : W.A.D.P.Wijerathna

Office : Ayagama Pradeshiya Sabha

Date : 2024.10.28

SCALE 1:10000

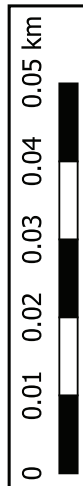

LEGEND

Roads




Ayagama PS Area

Road Start


Nikagoda Aludeniya Road

SG/APS/B034/45/05




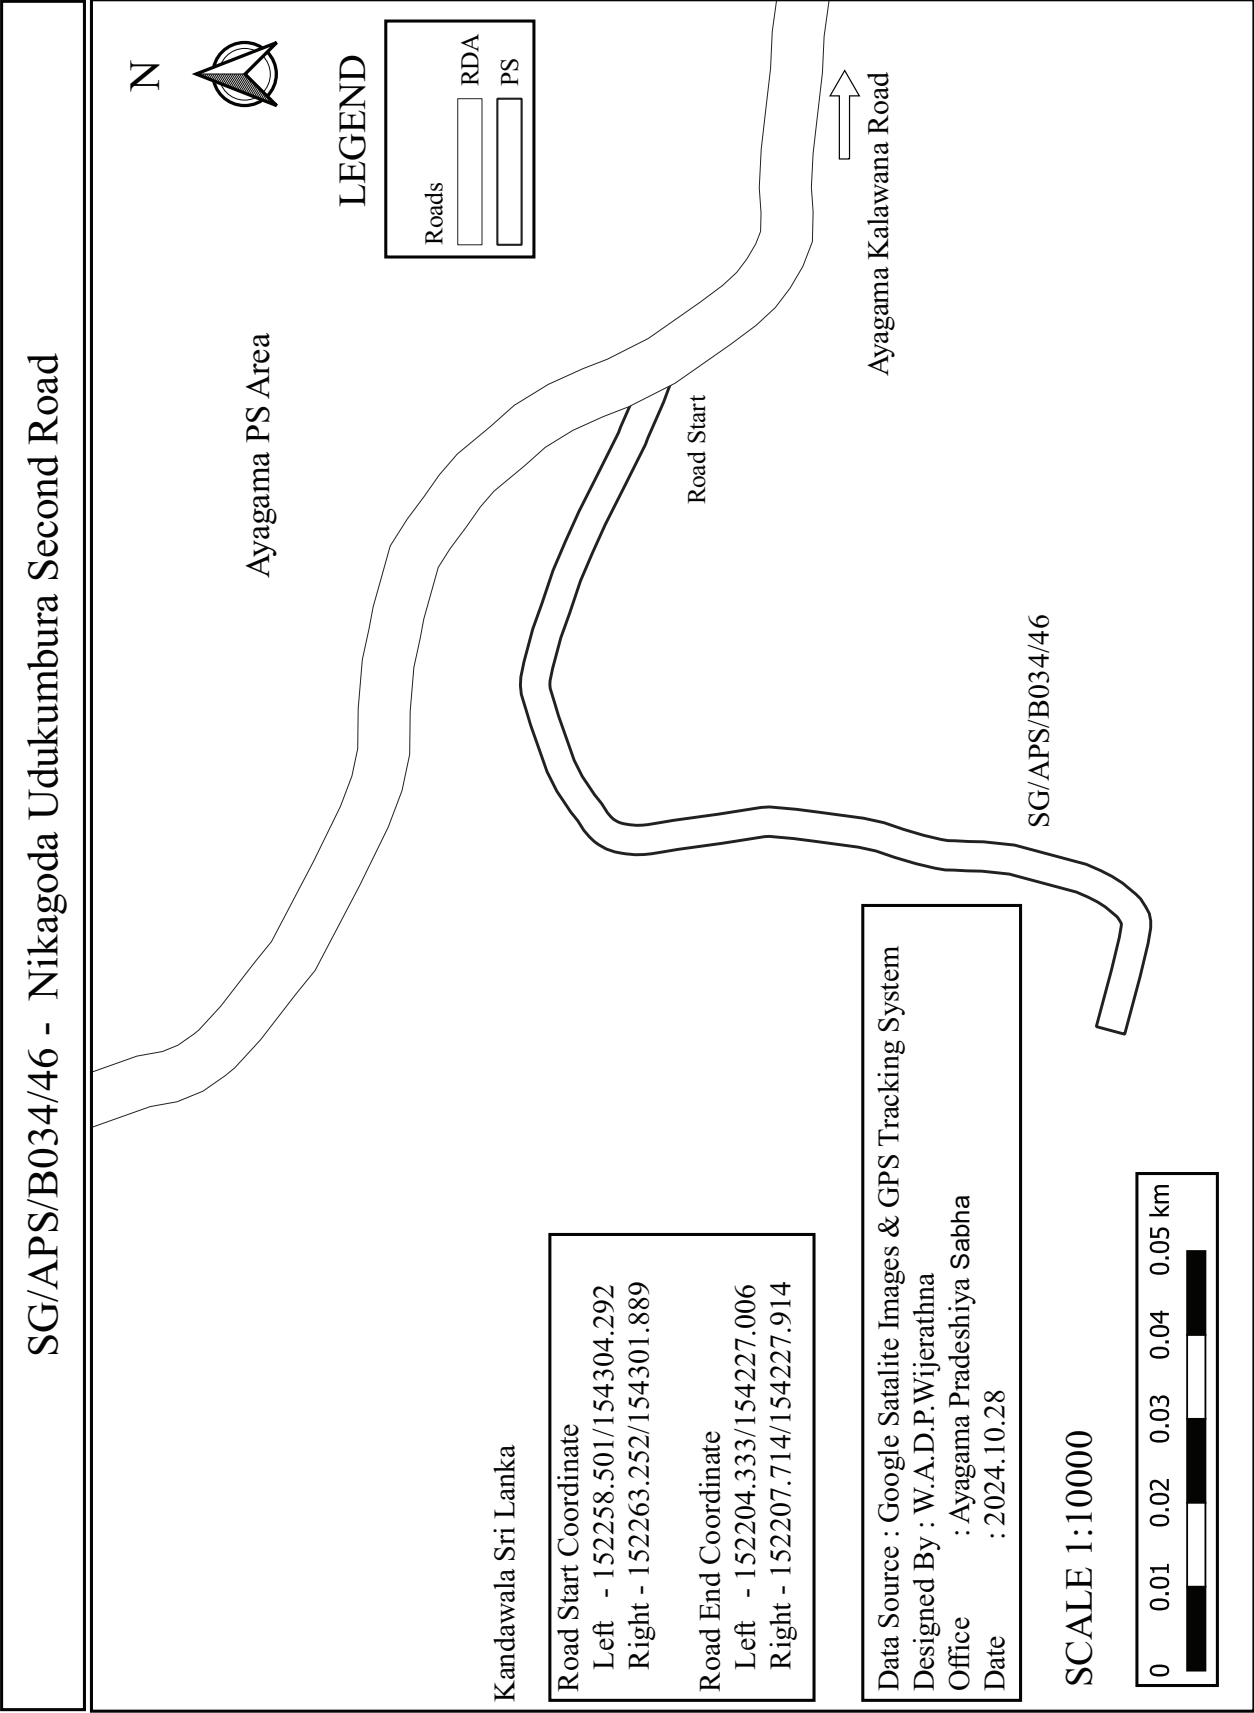


SG/APS/B034/47 - Nikagoda Udukumbura Third Road

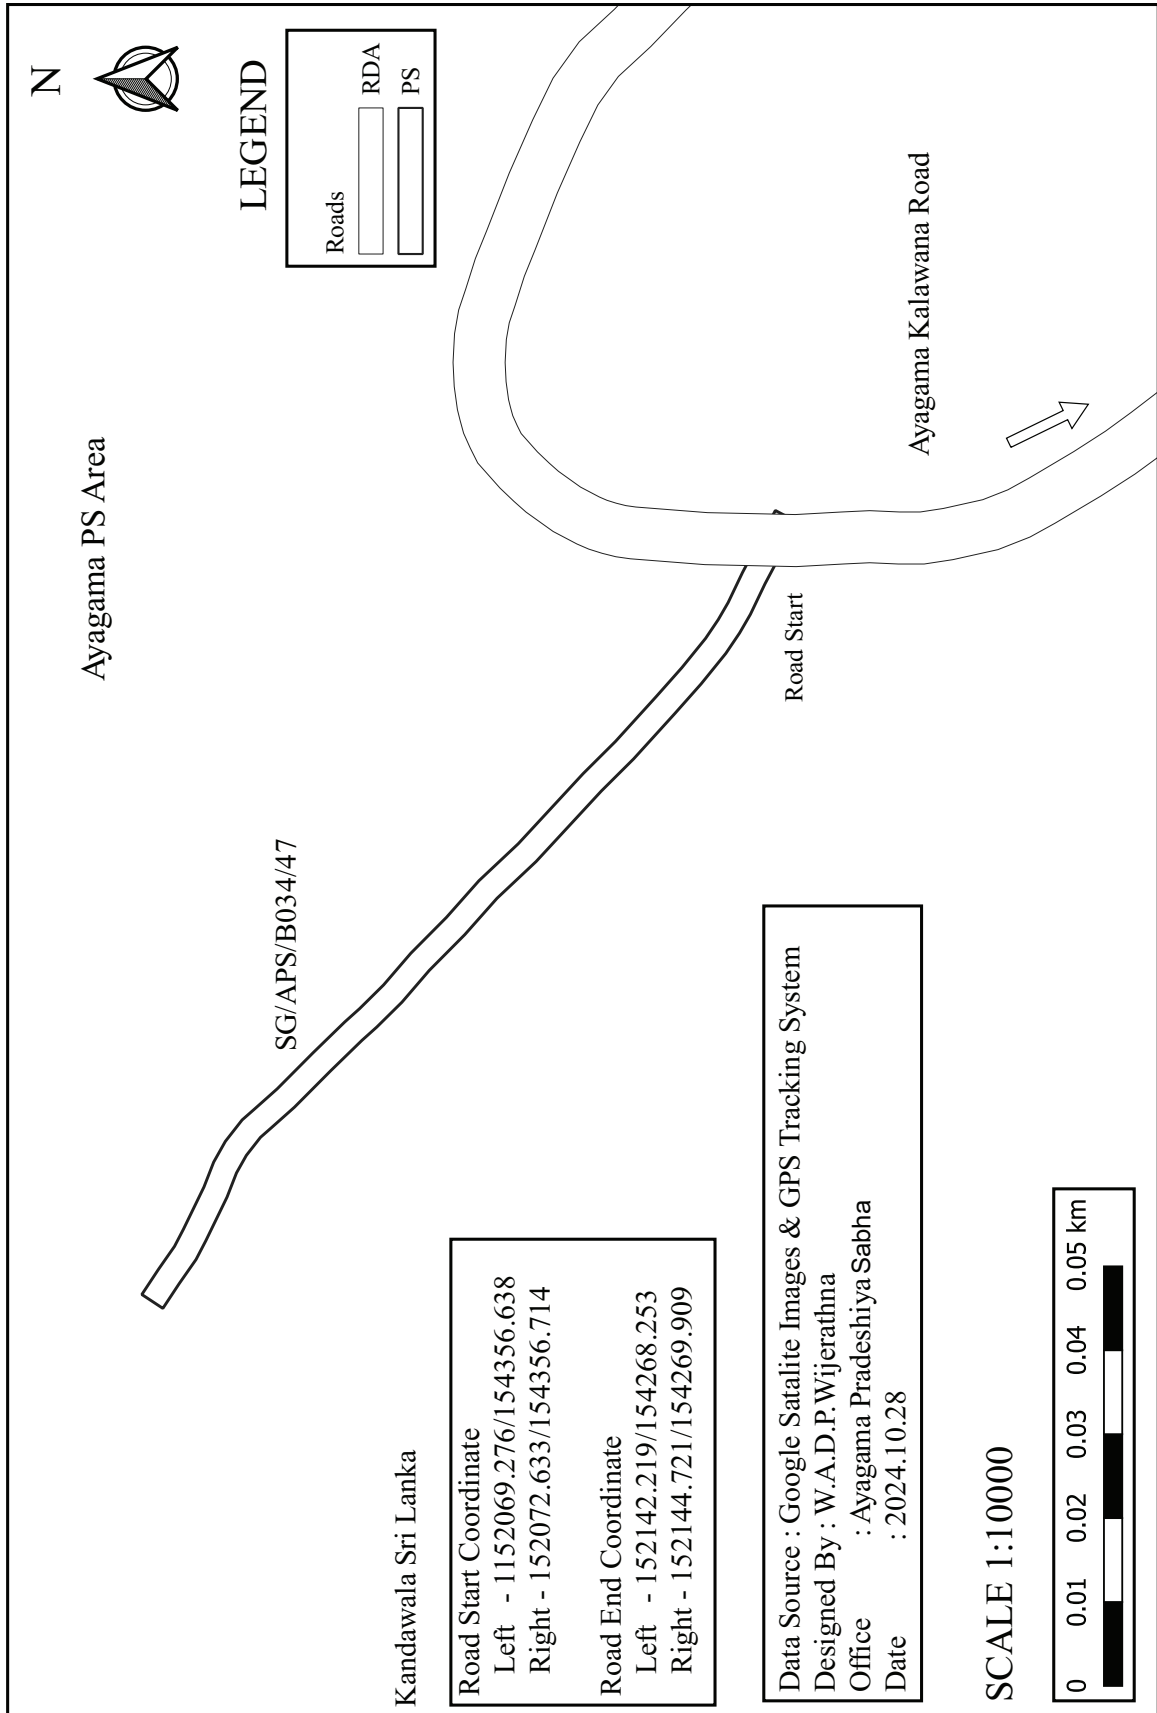



Kandawala Sri Lanka

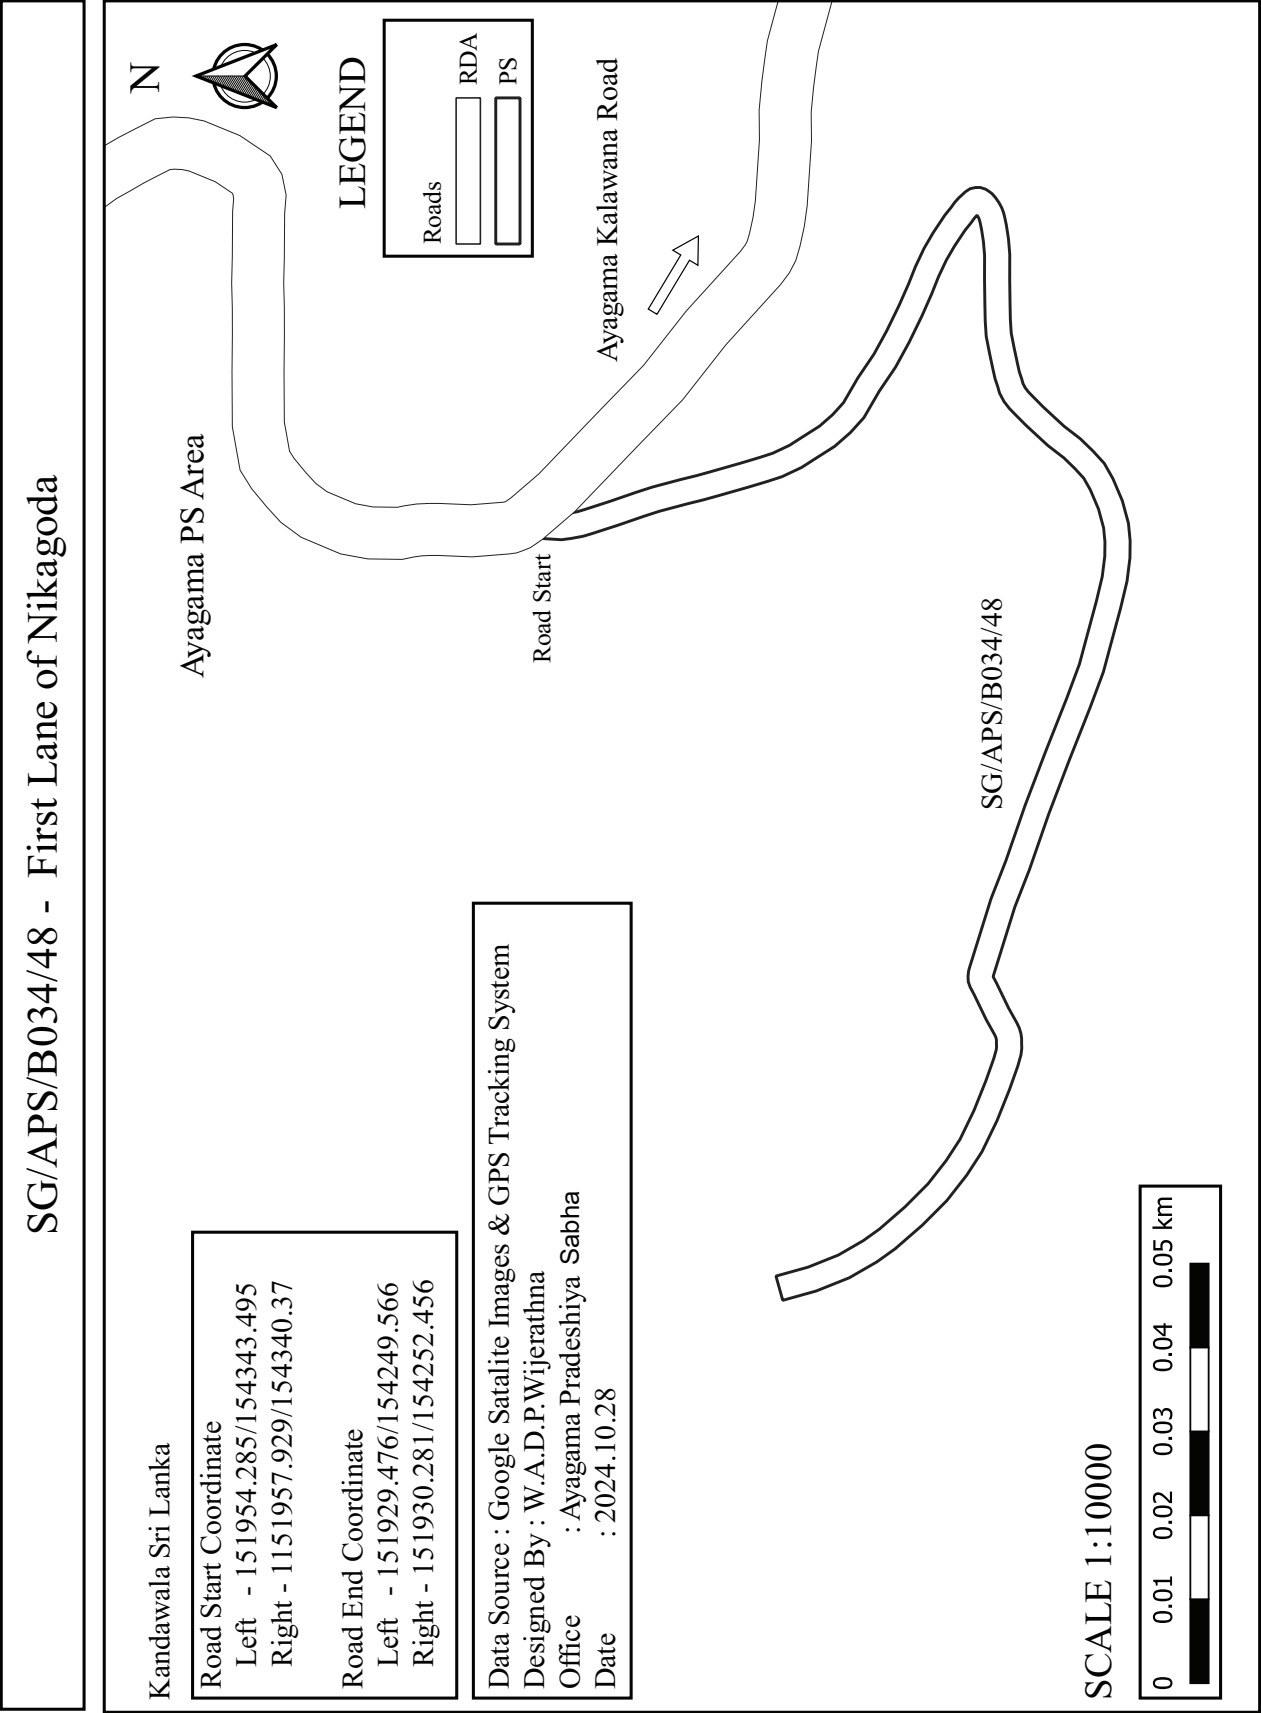



SG/APS/B034/49 - Akkara 08 Ellakadewaththa Road

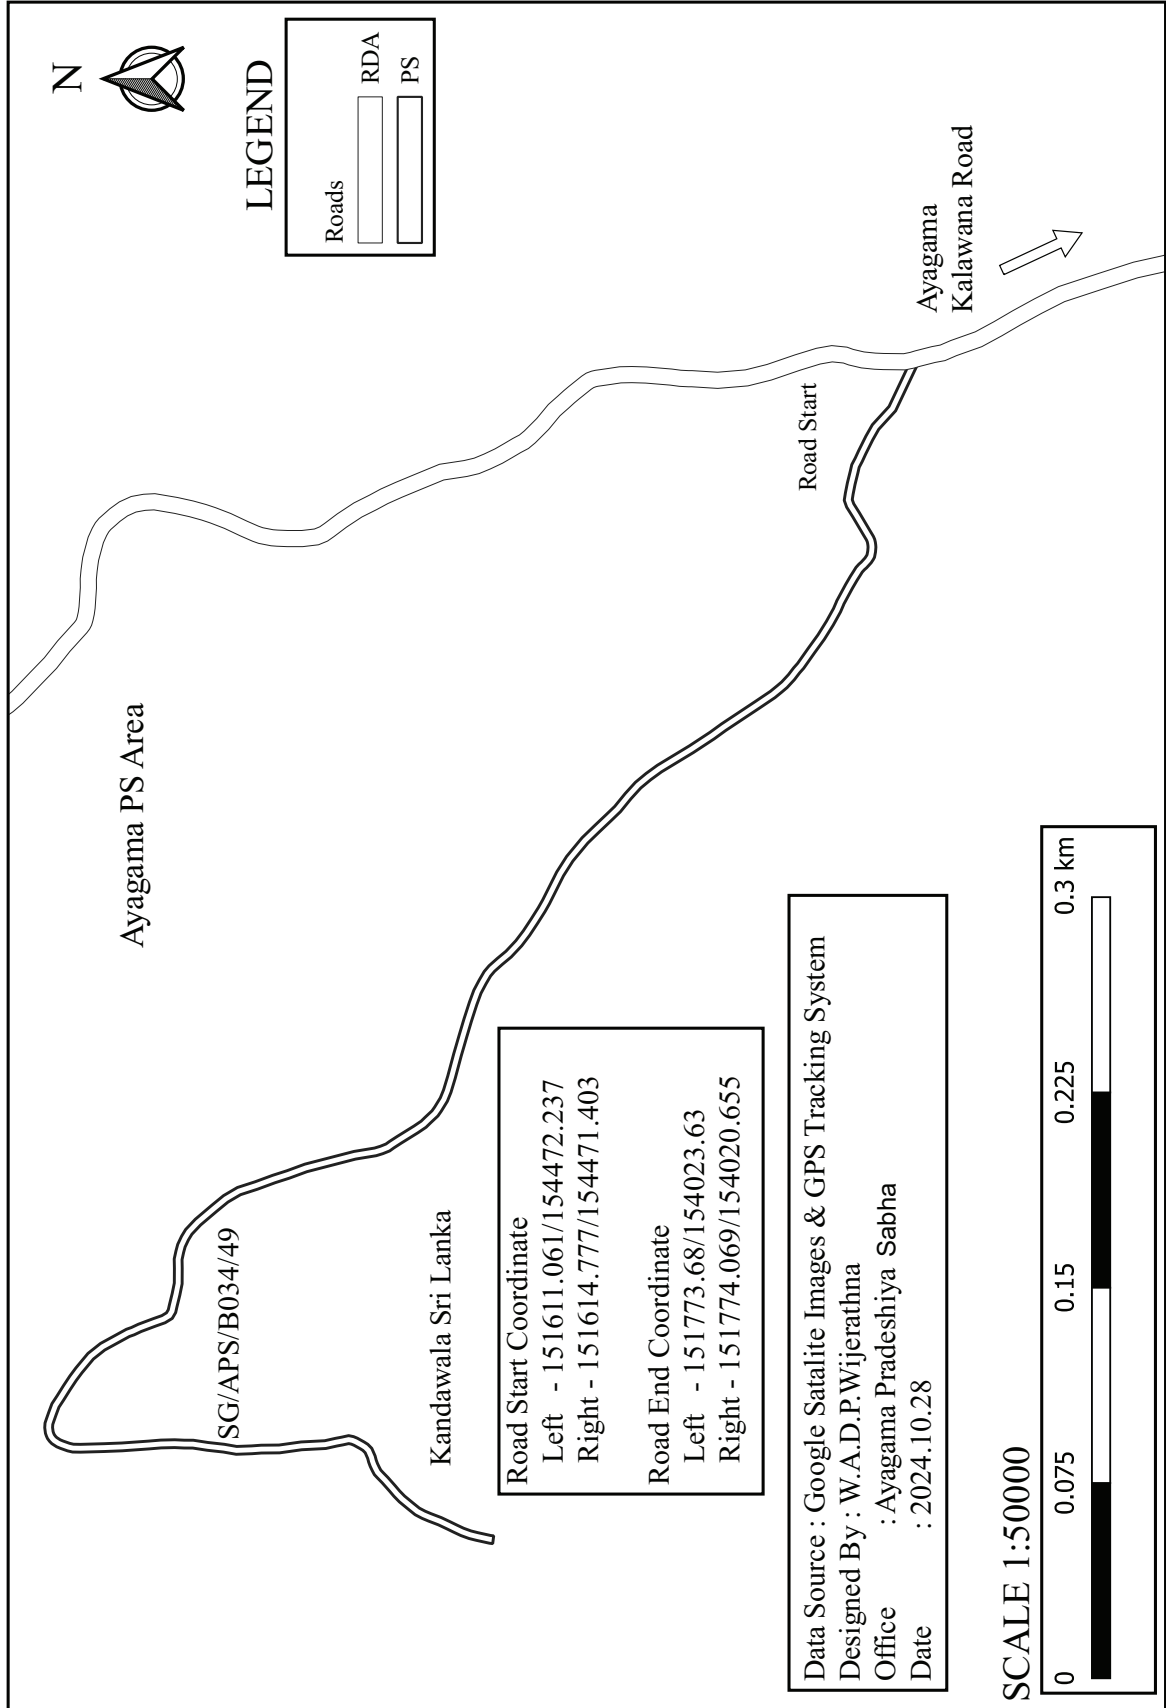


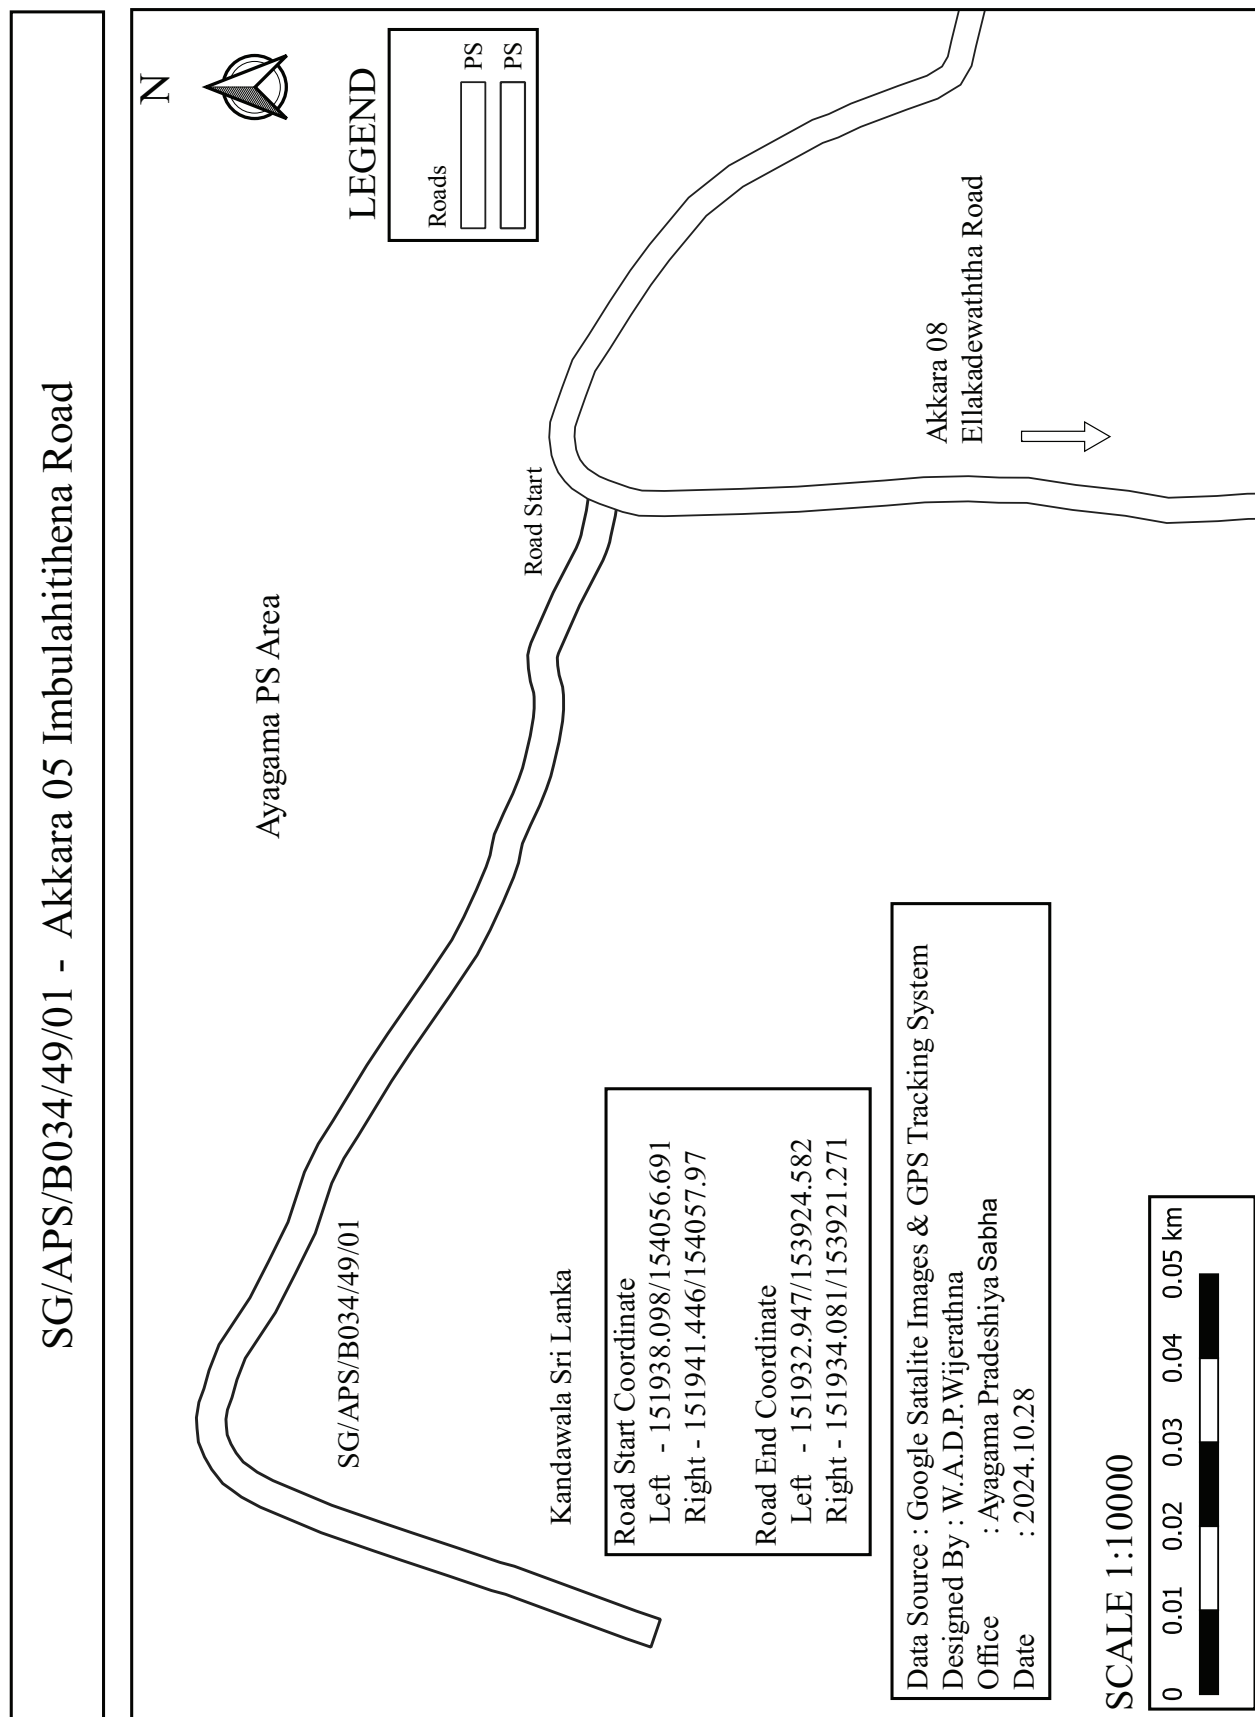


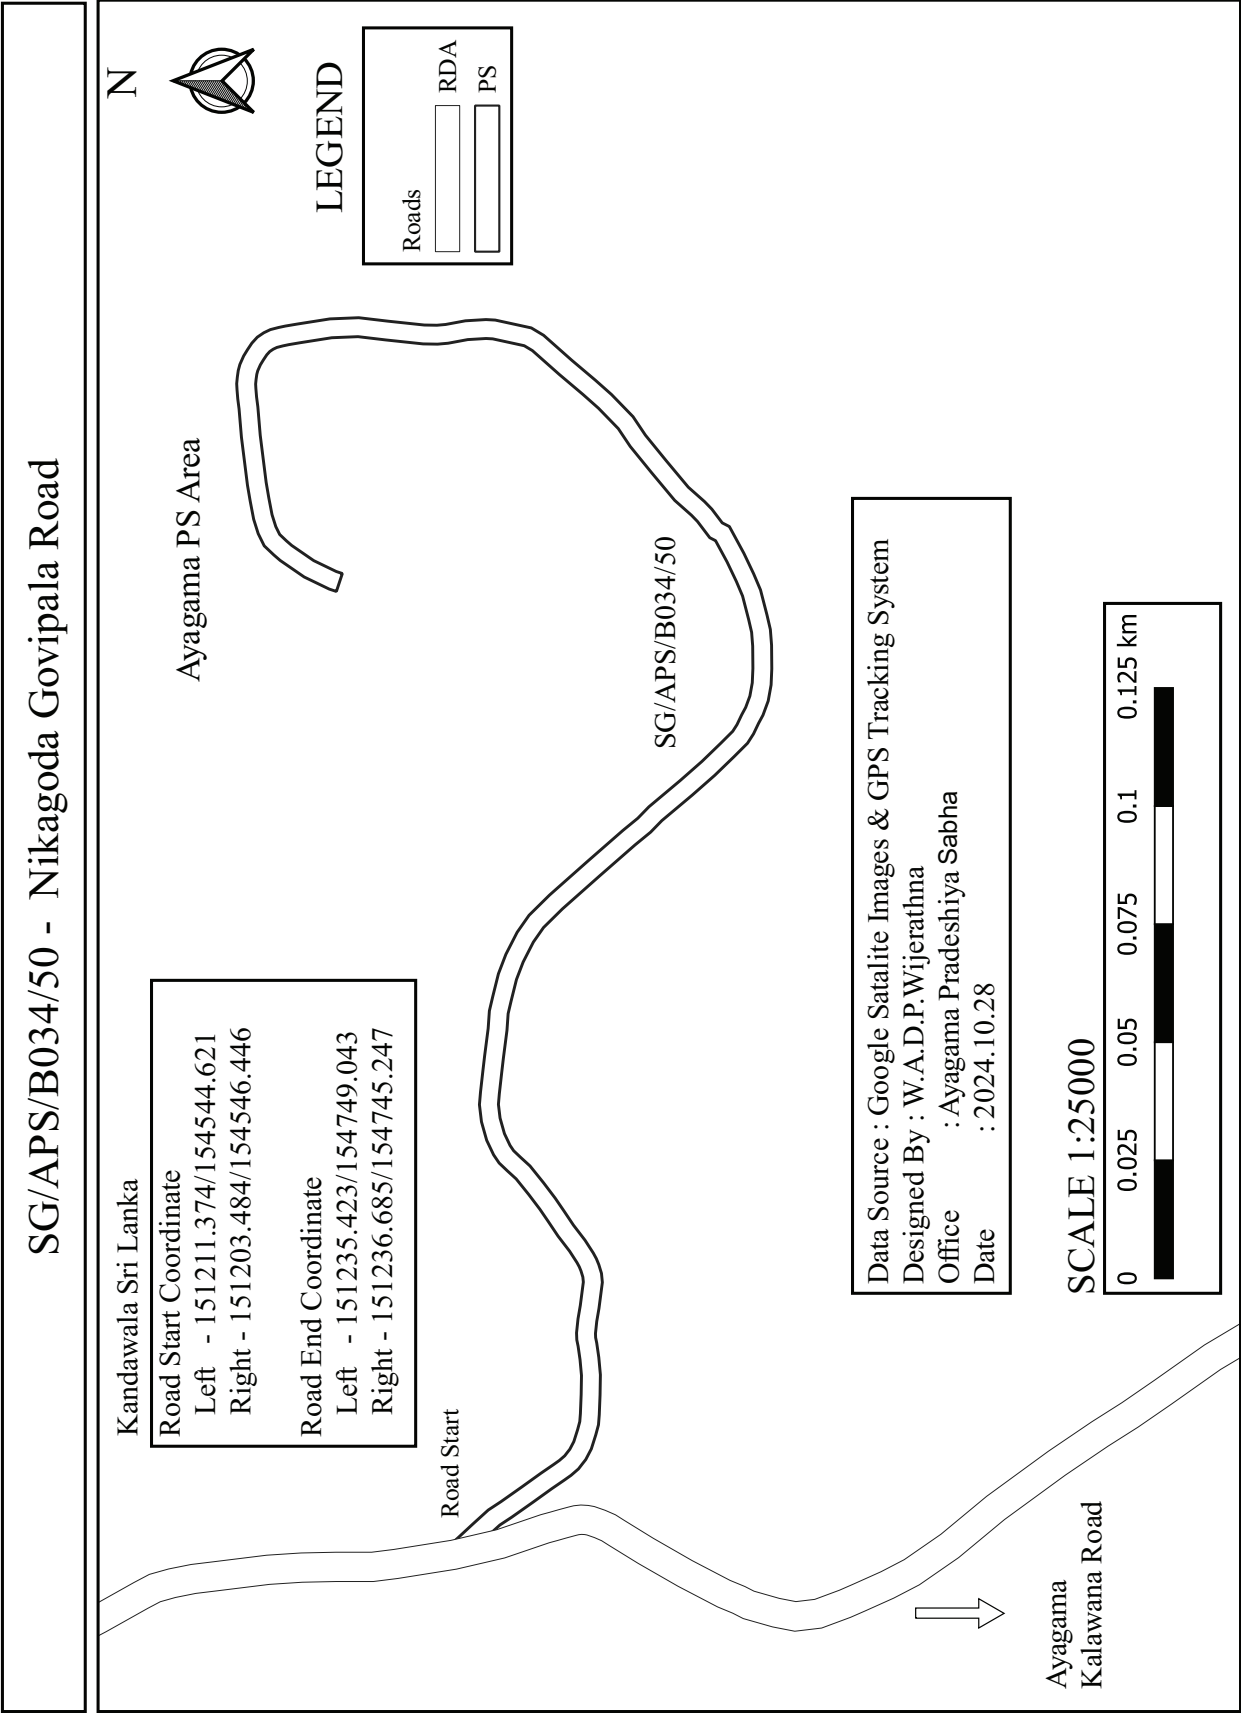


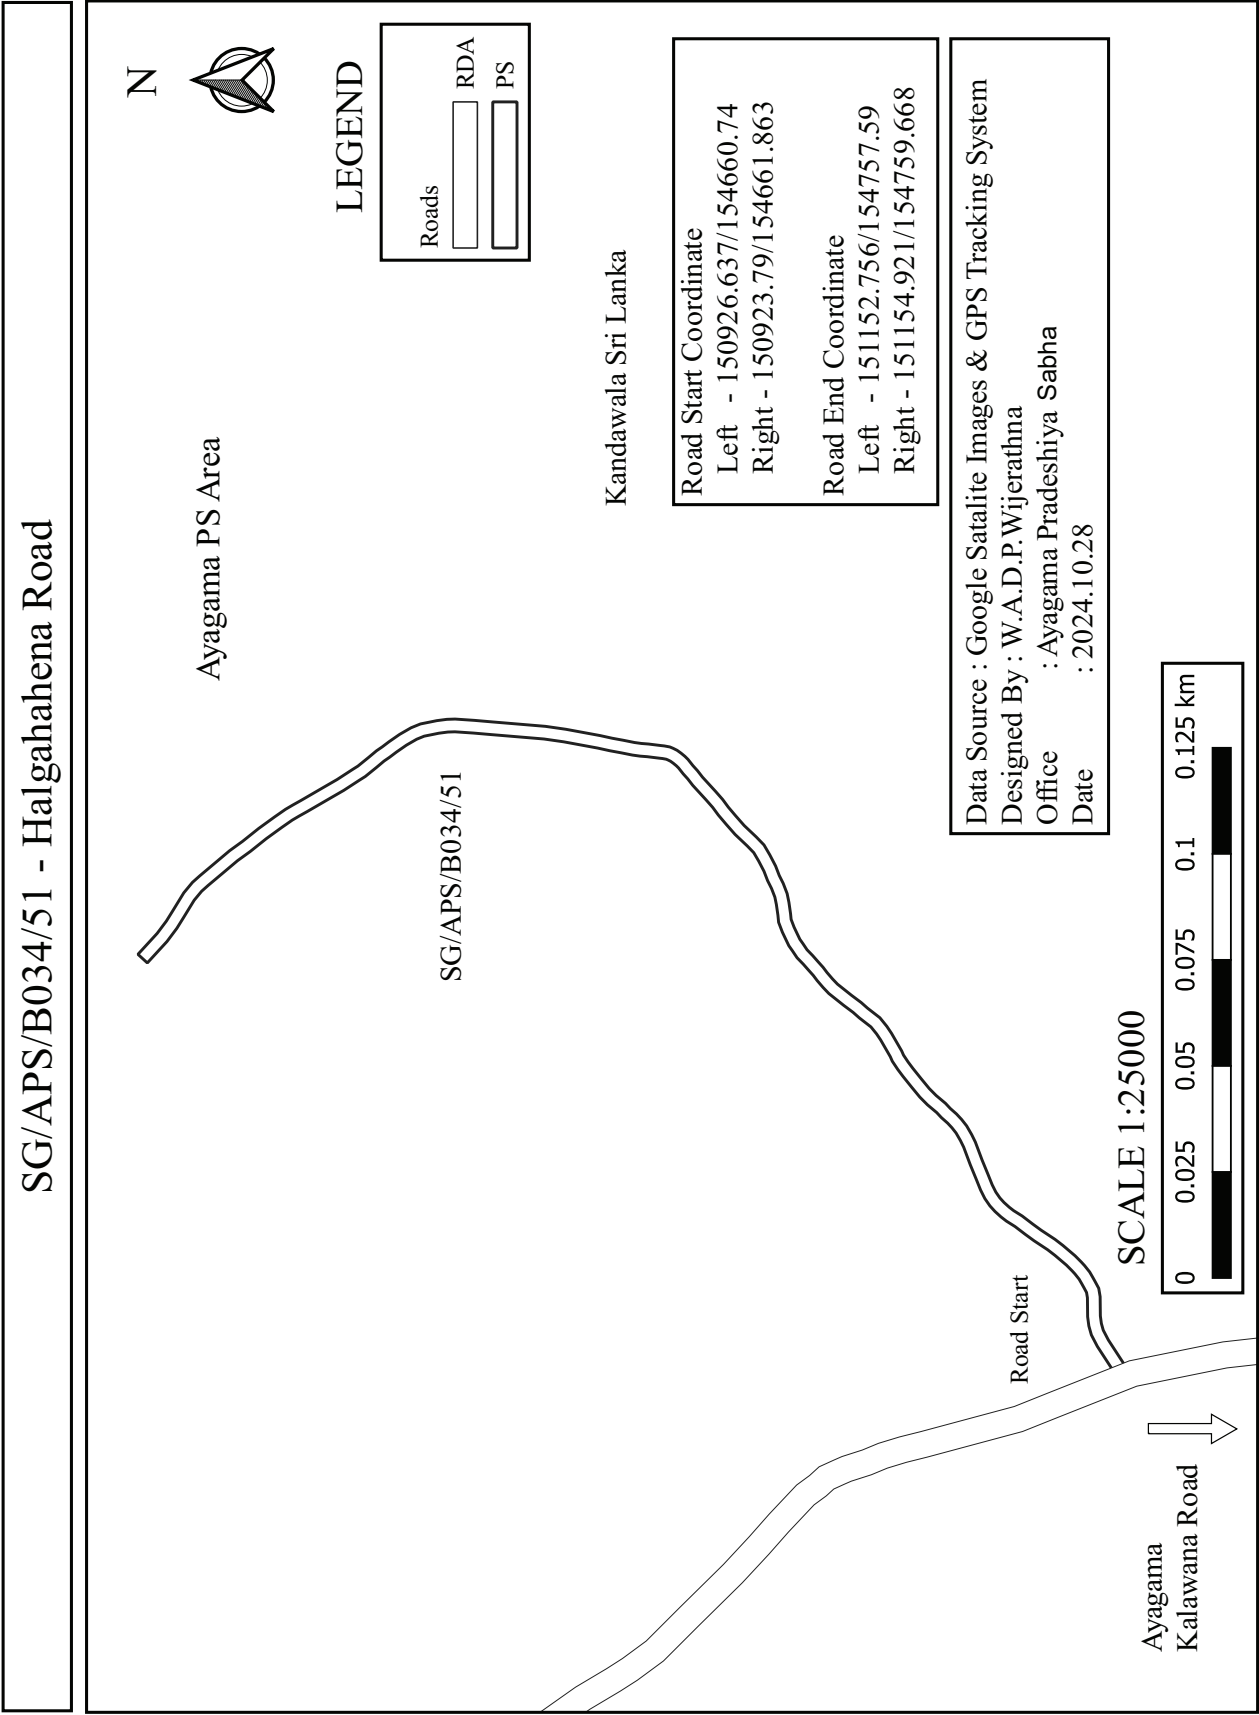

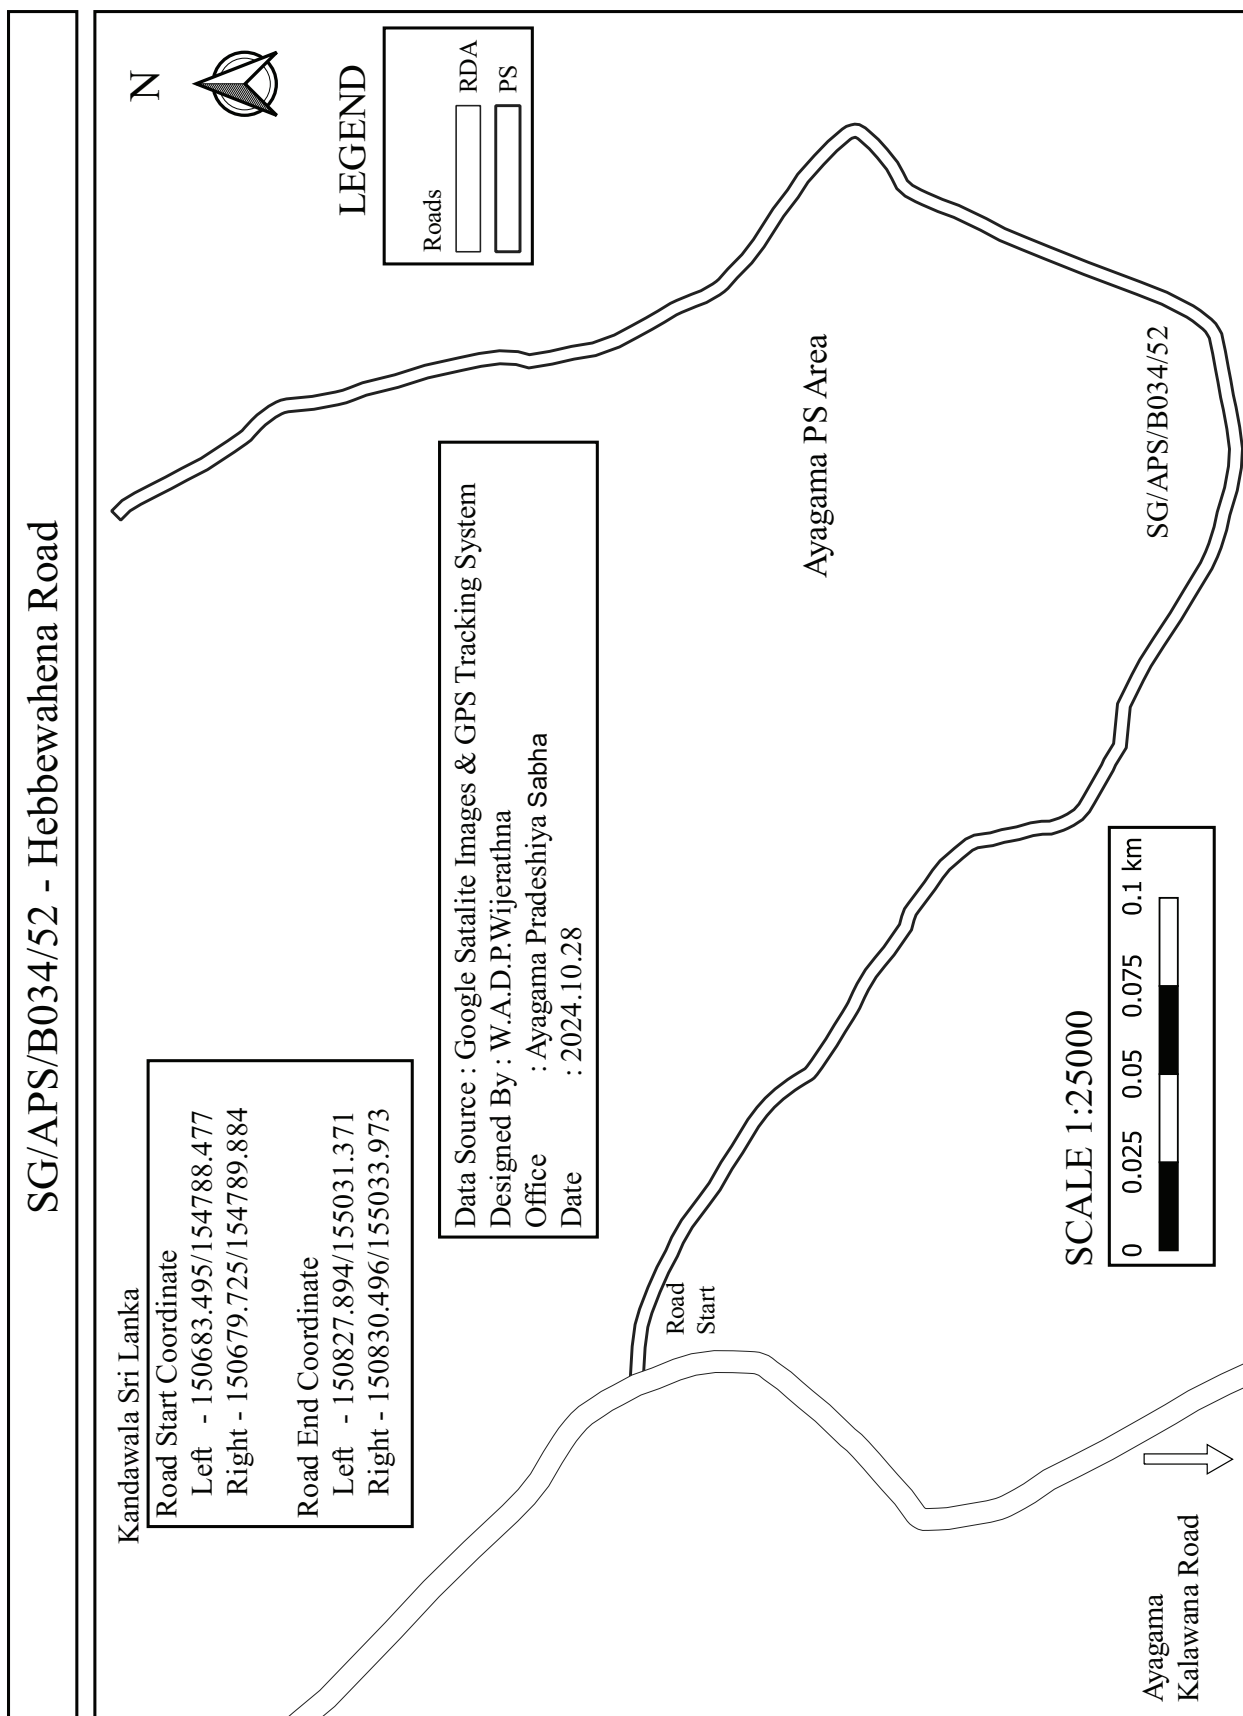


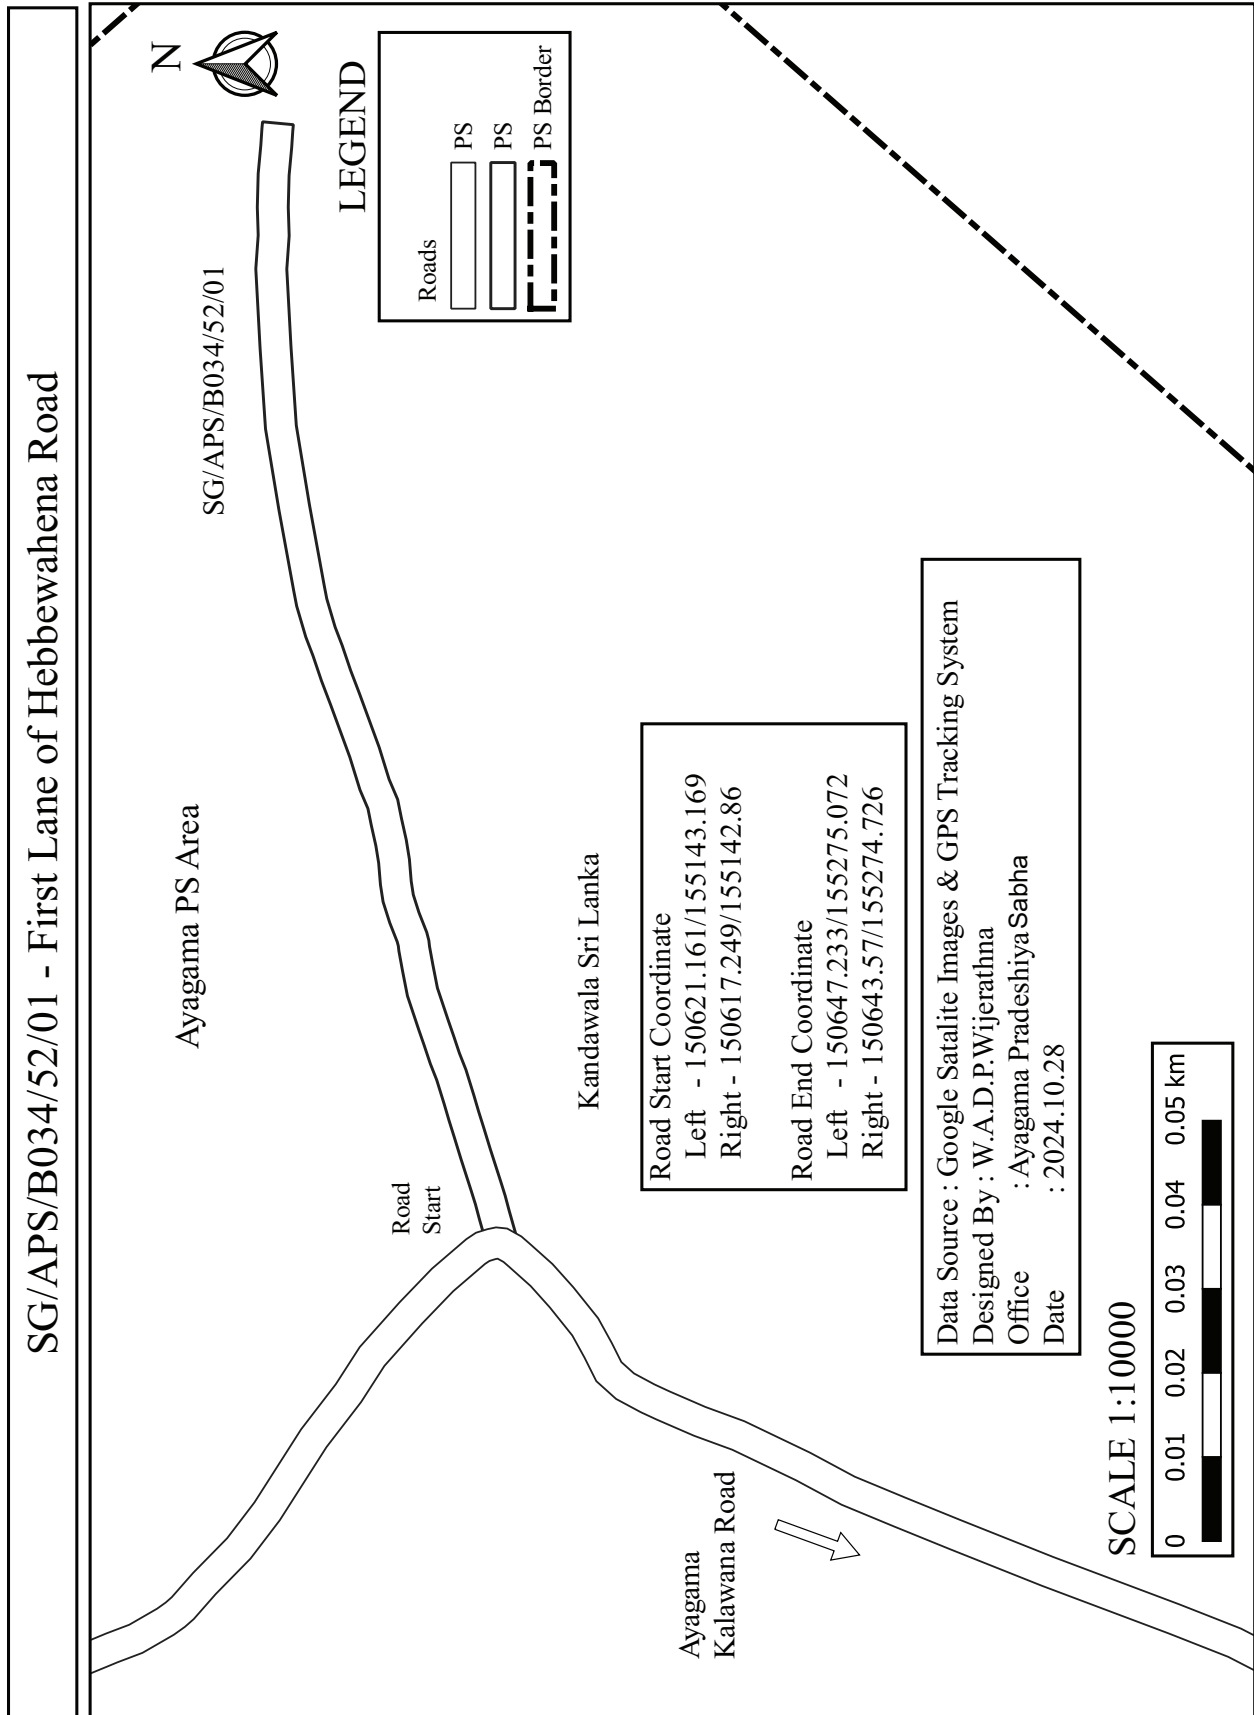


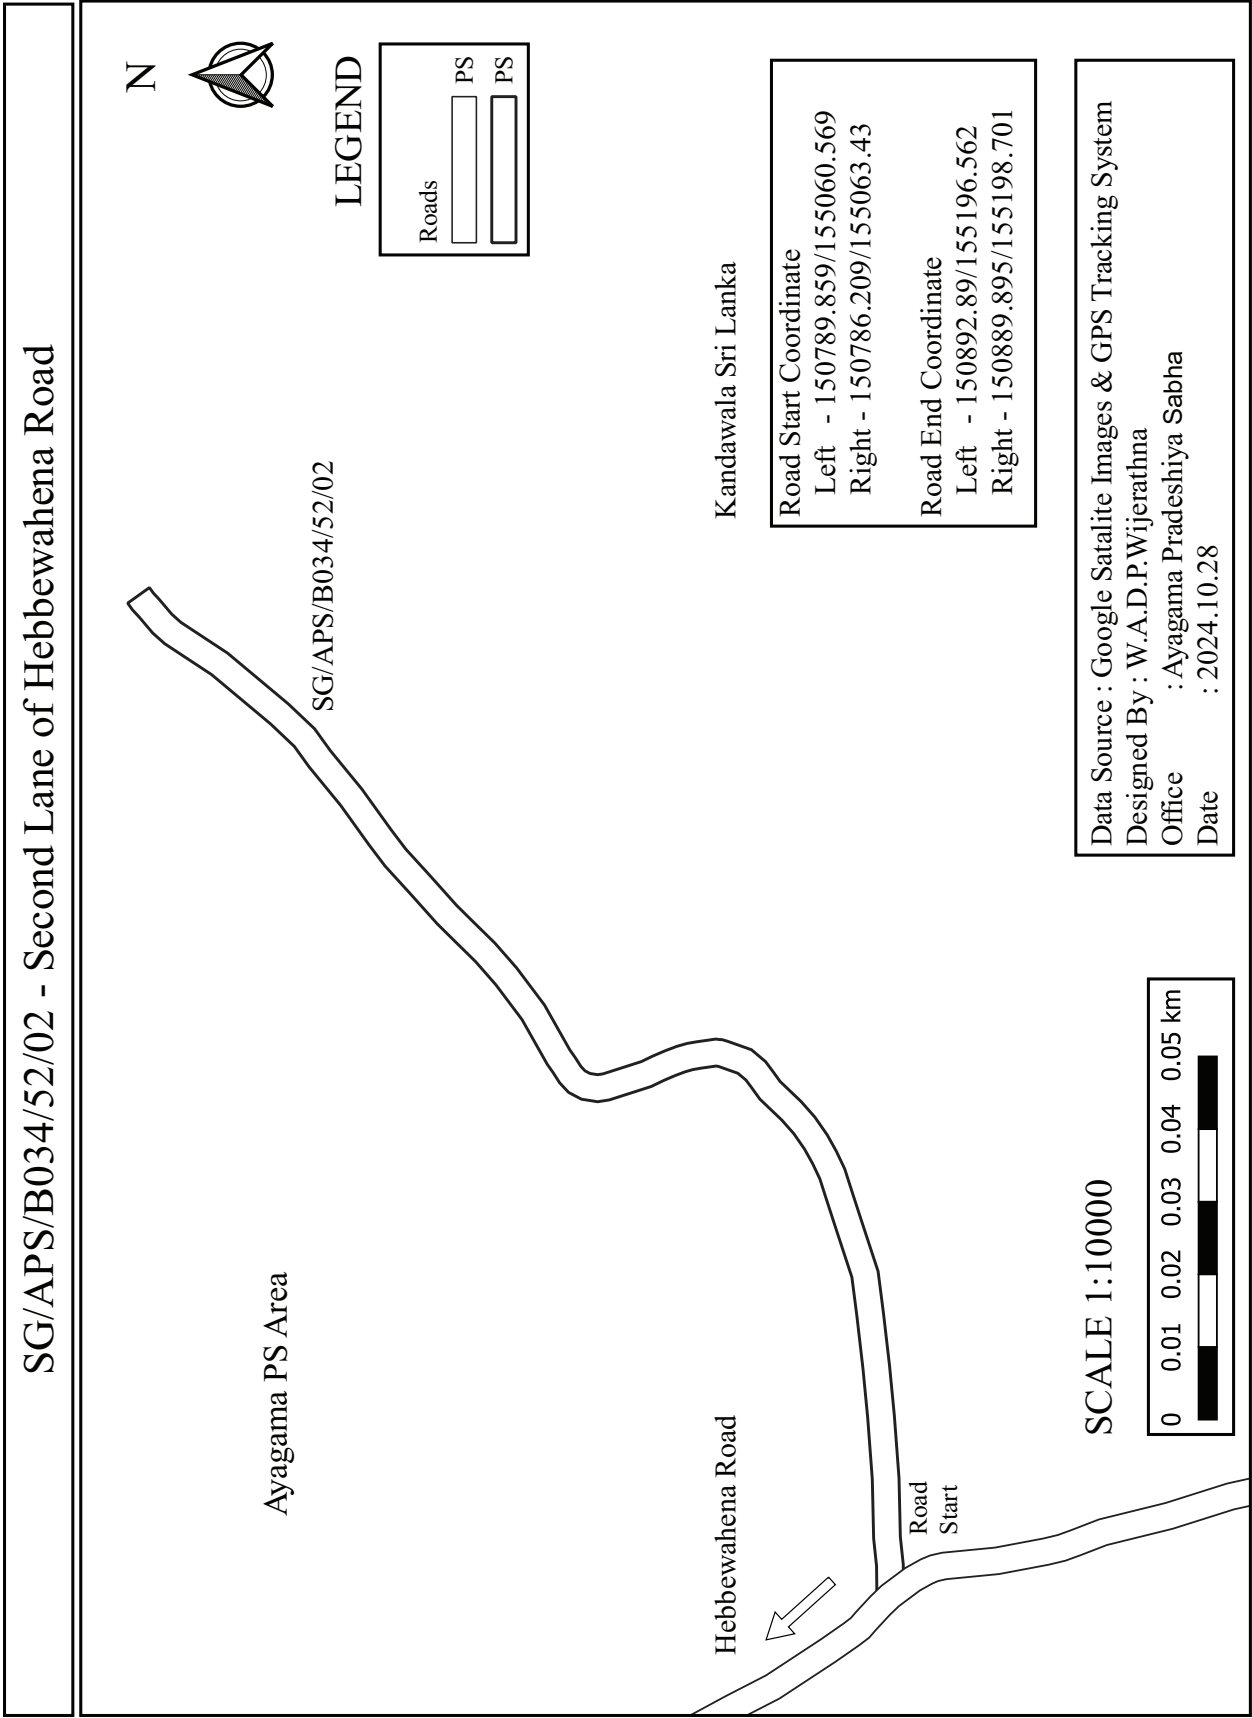


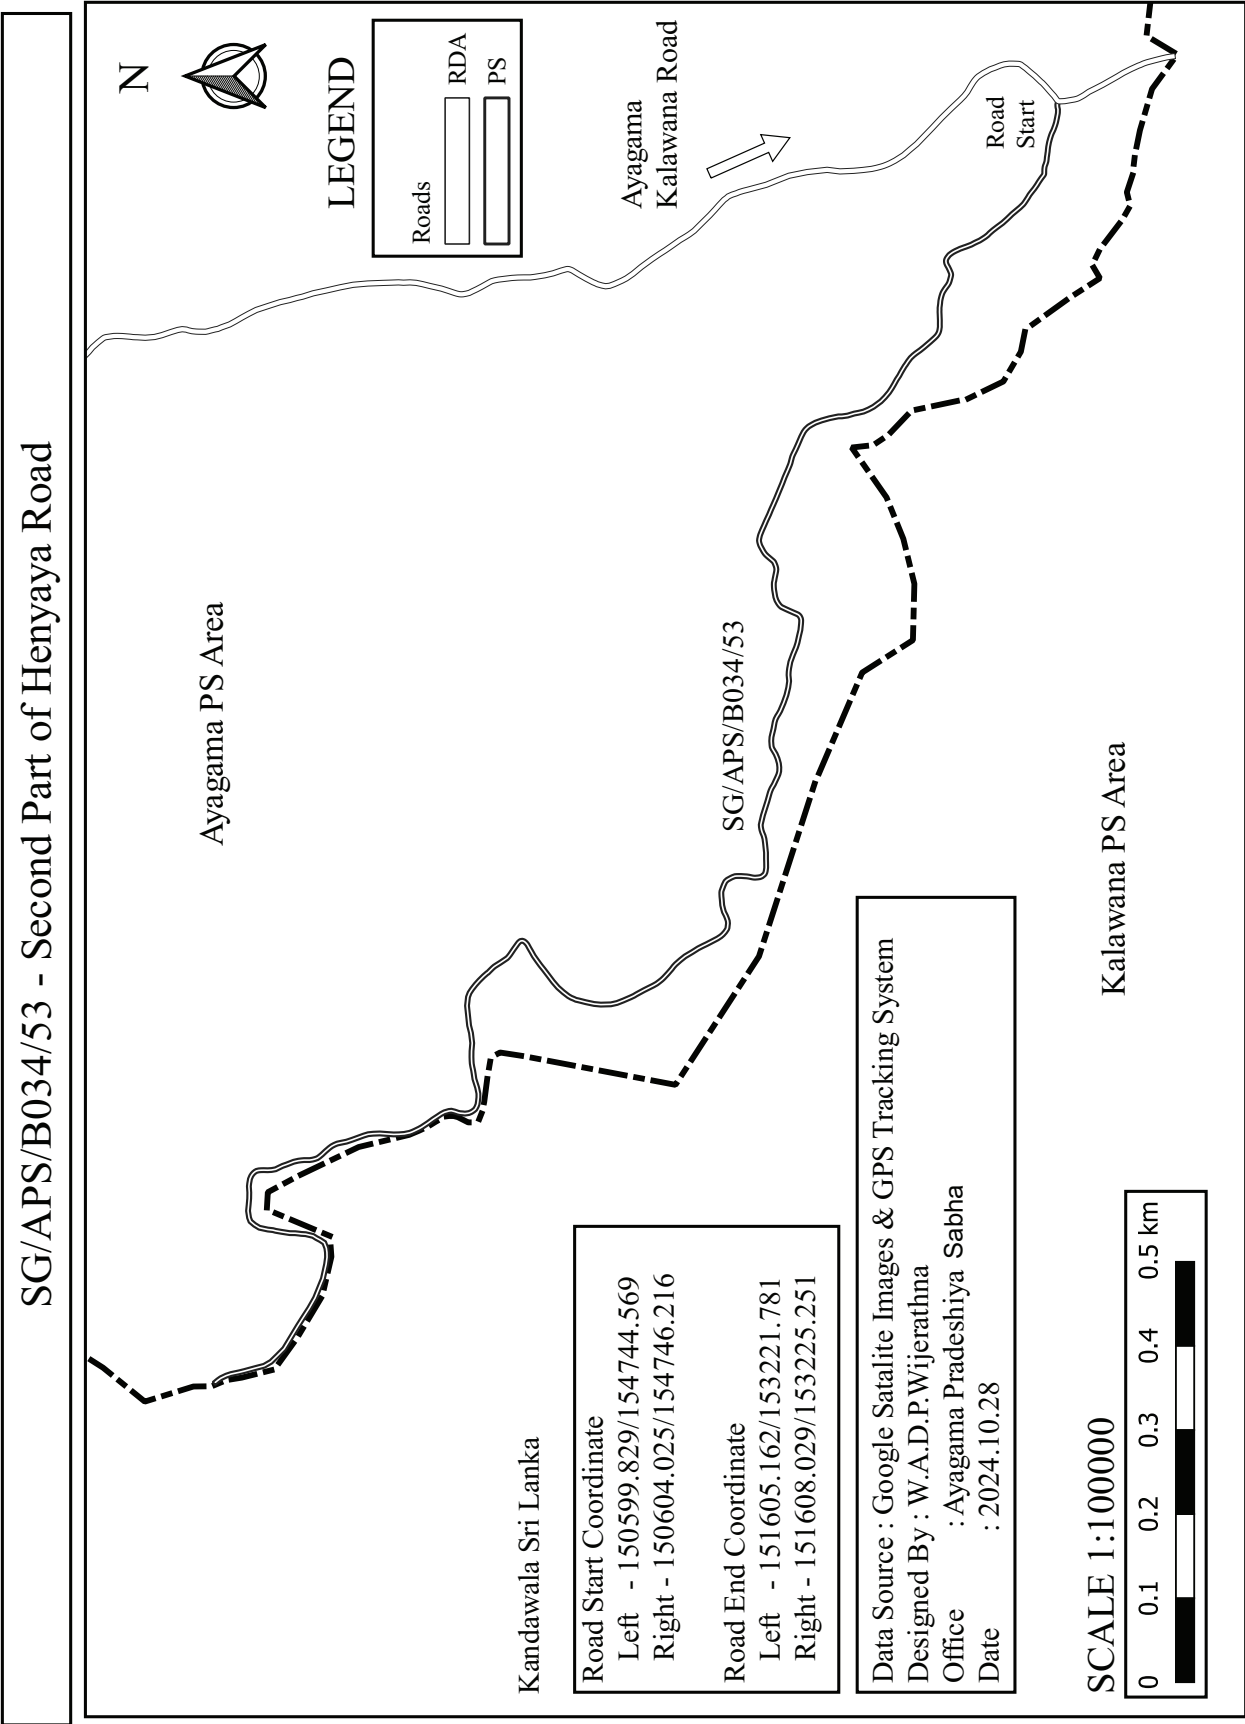



SG/APS/B034/53/01 - First Lane of Second Part of Henyaya Road

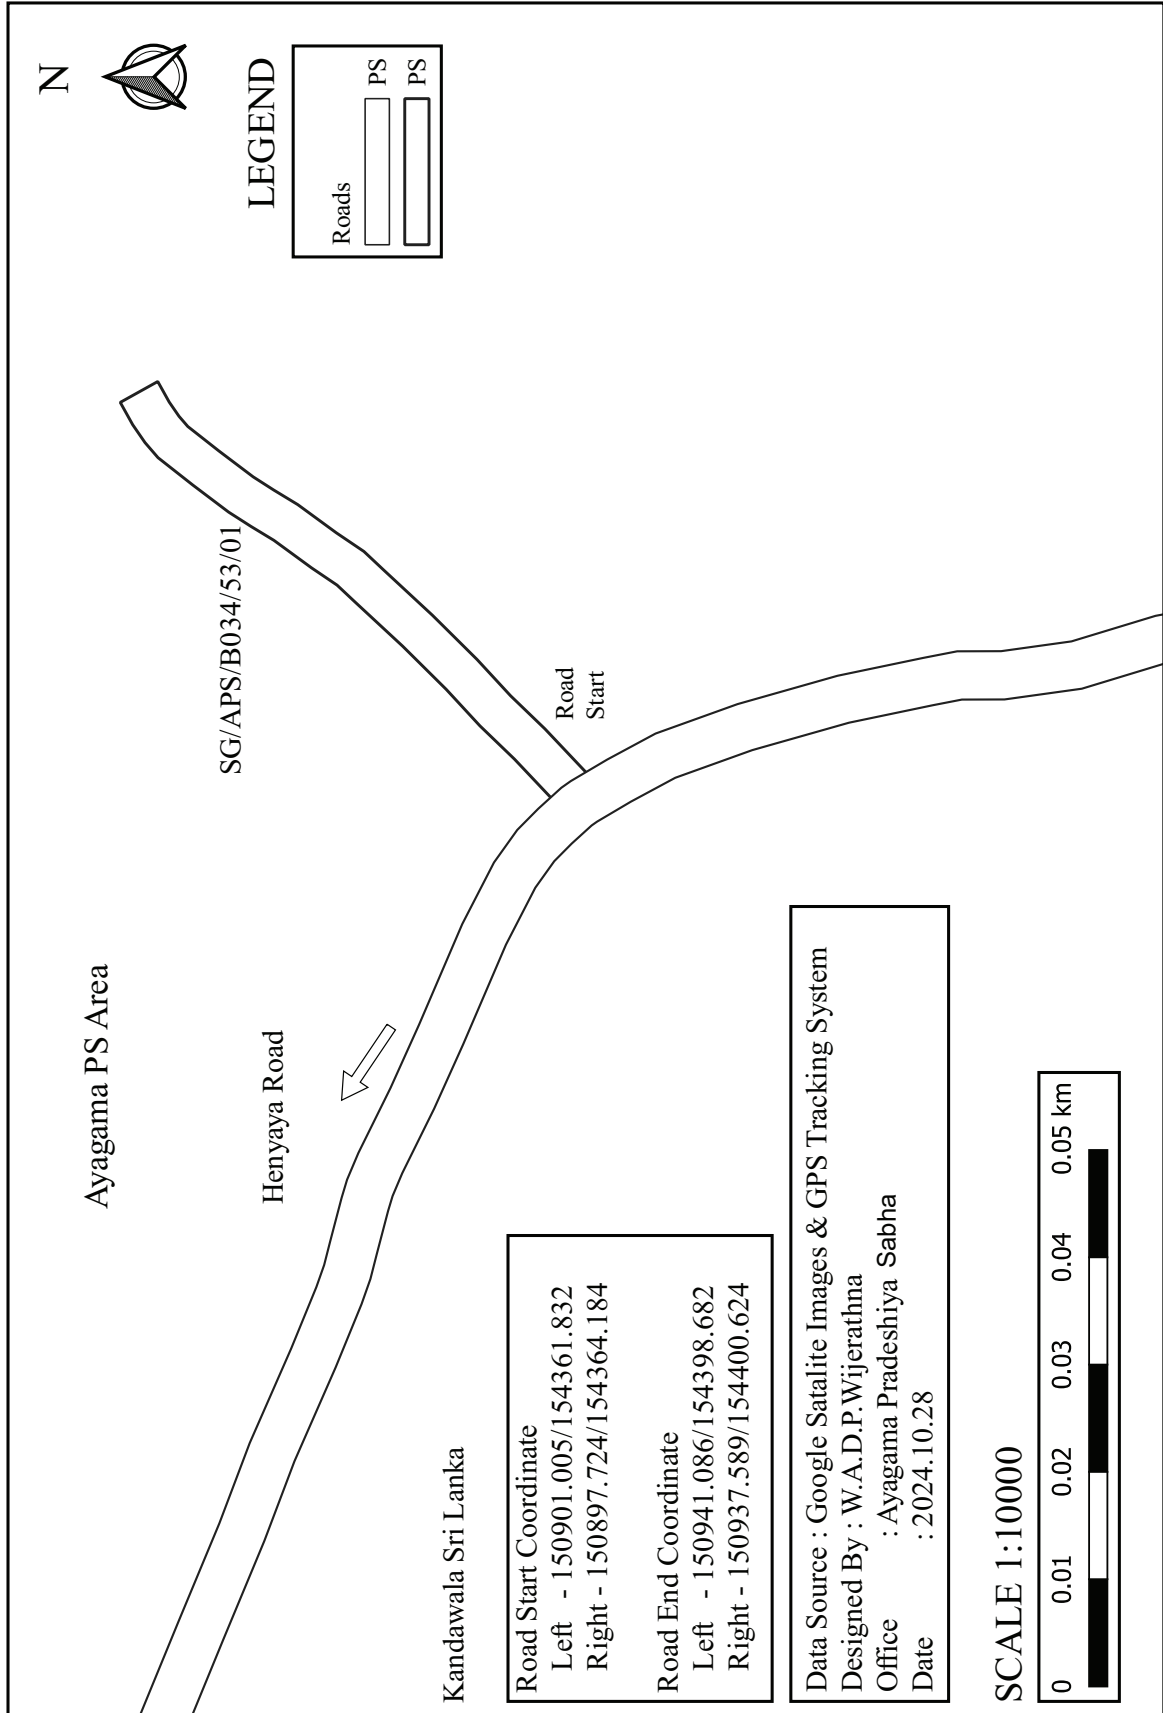


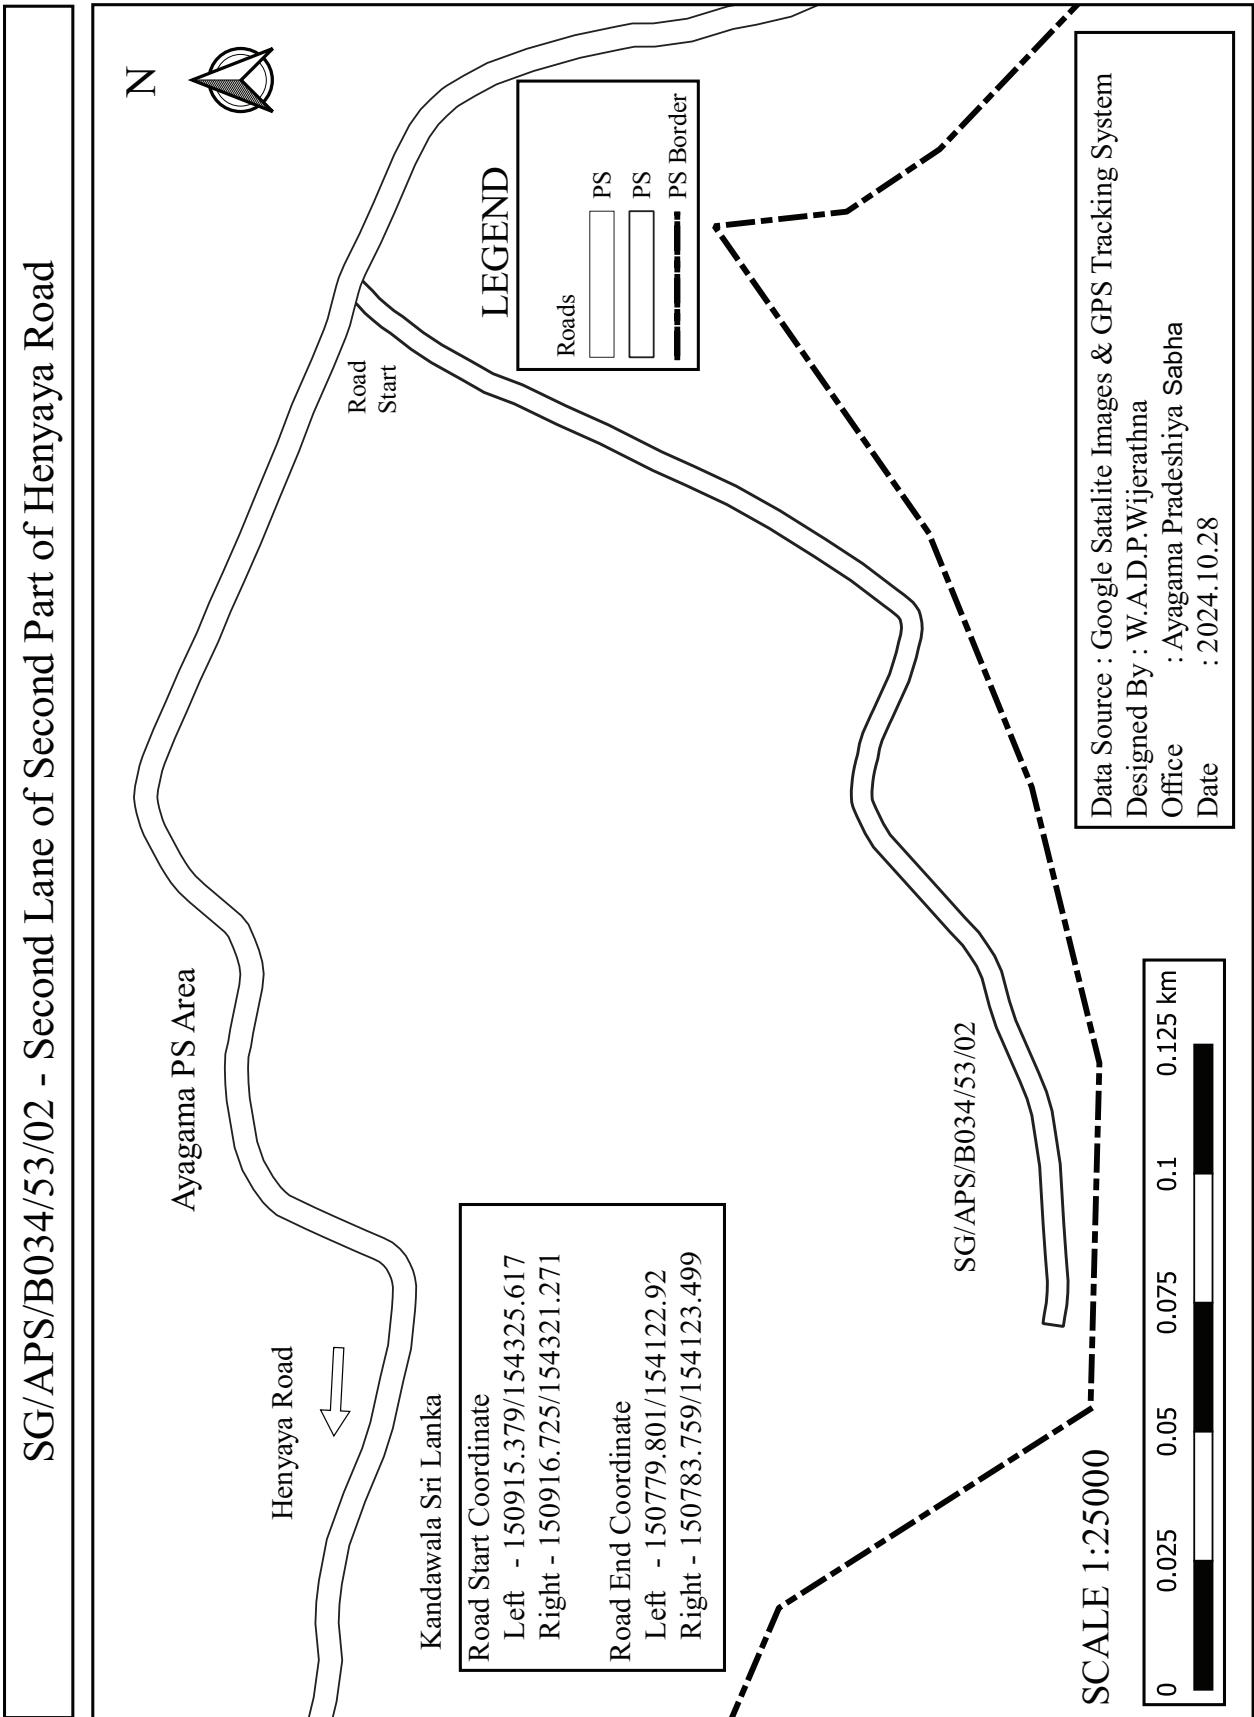


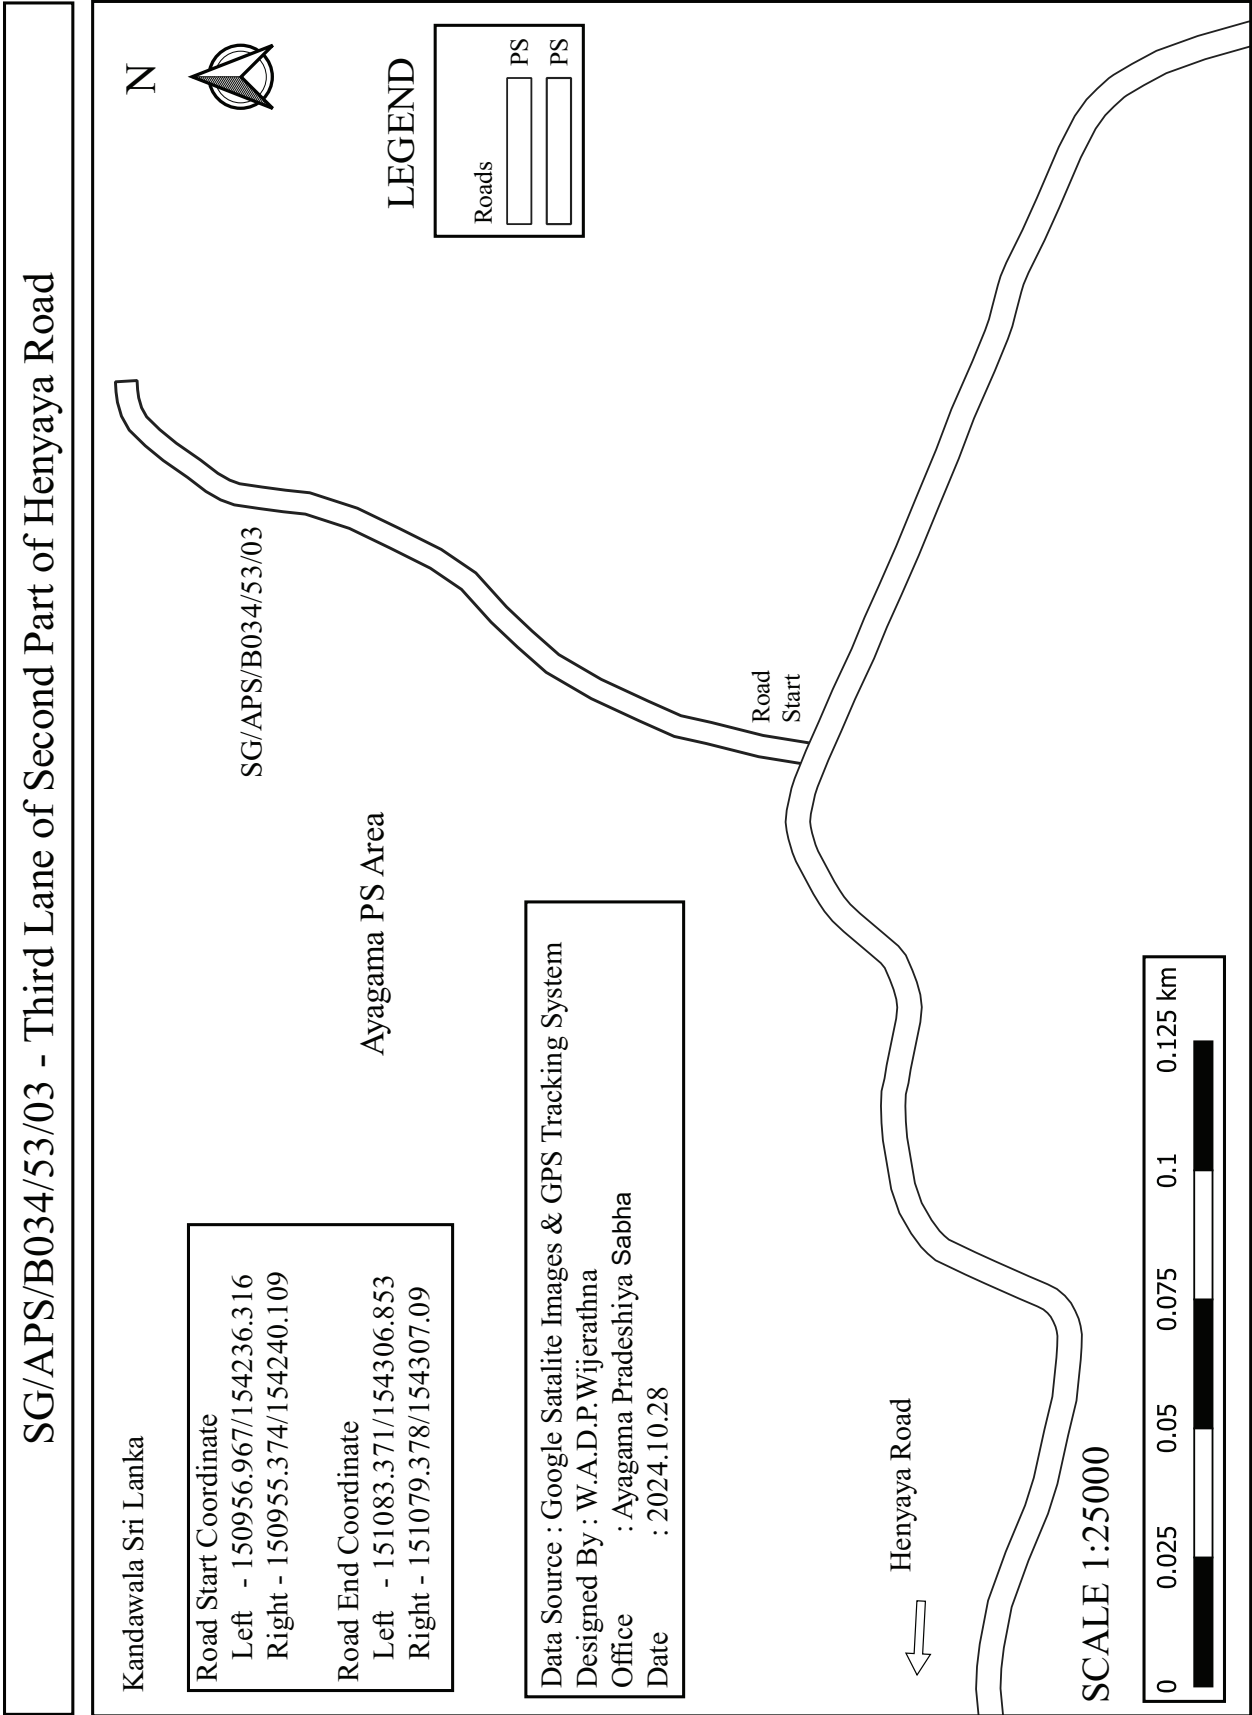


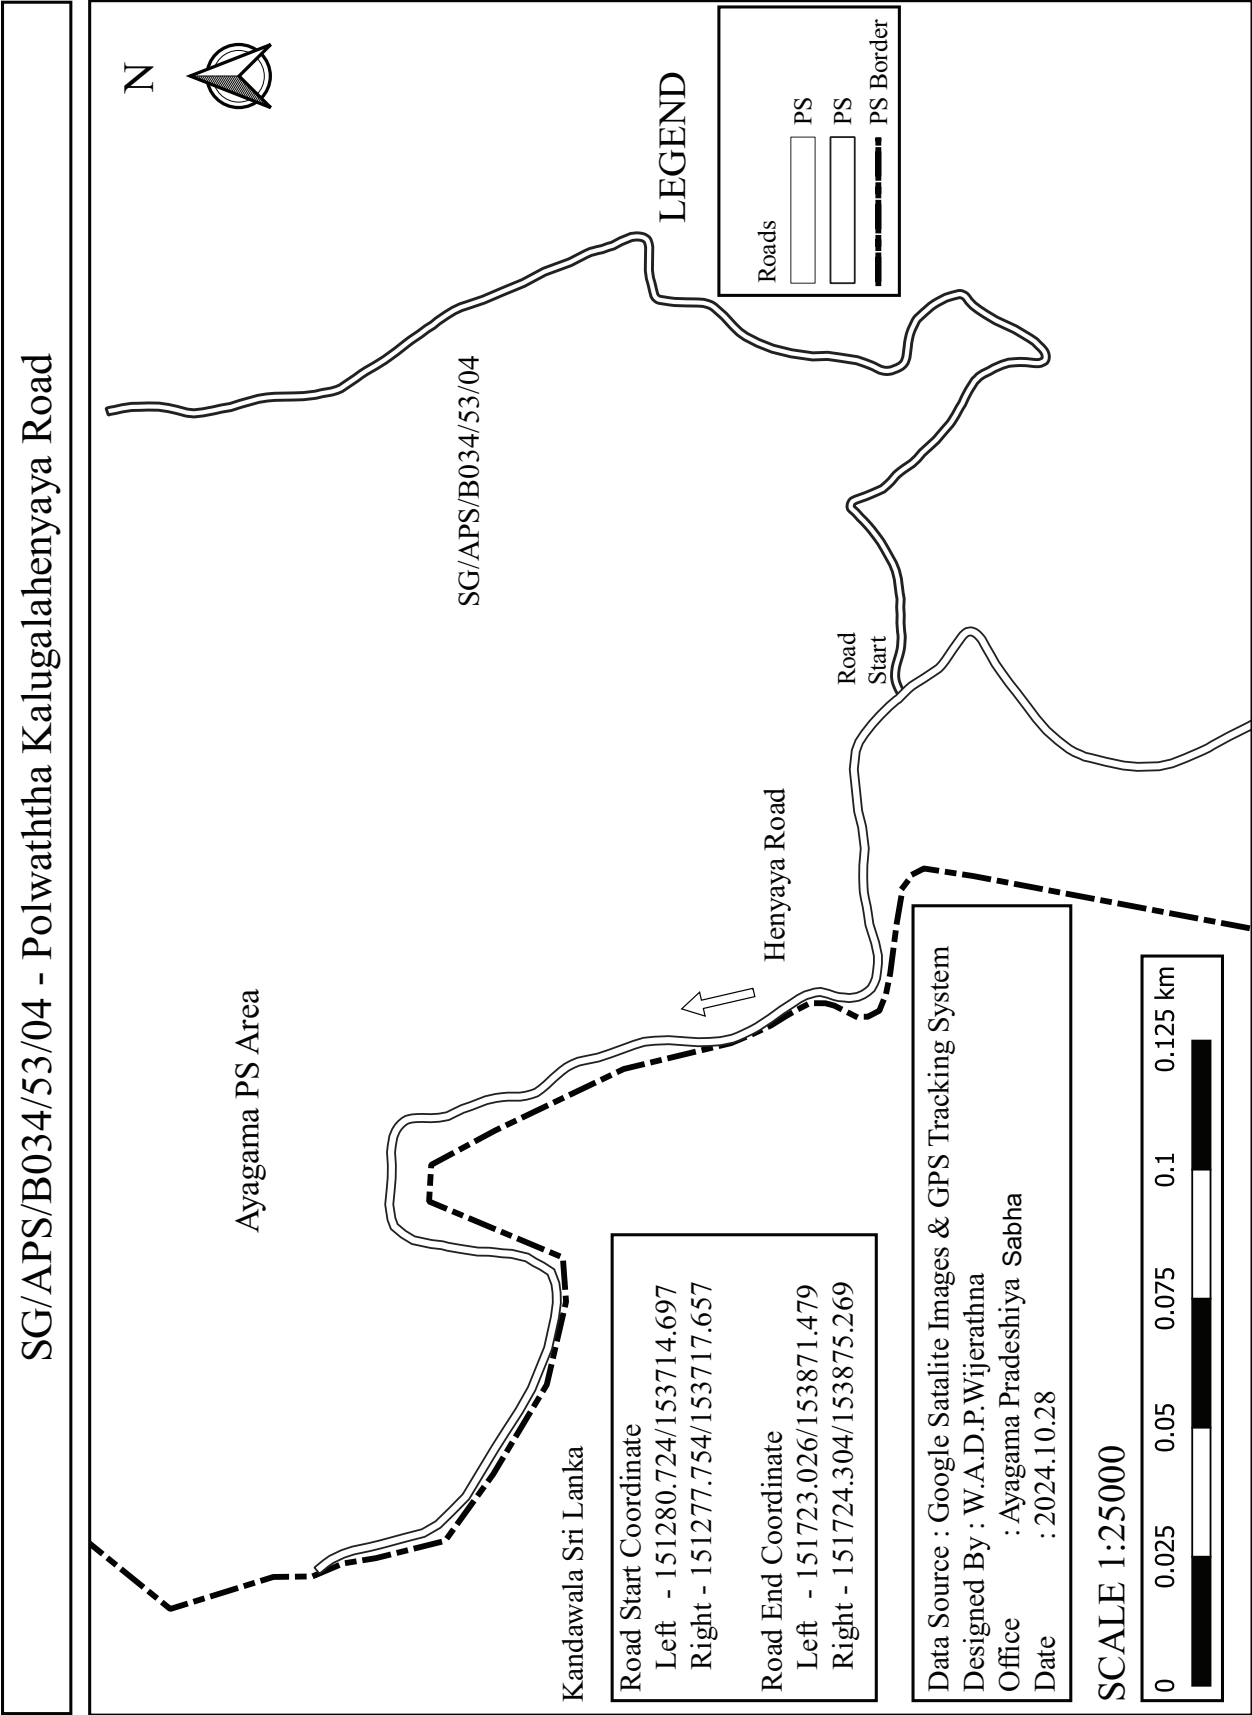


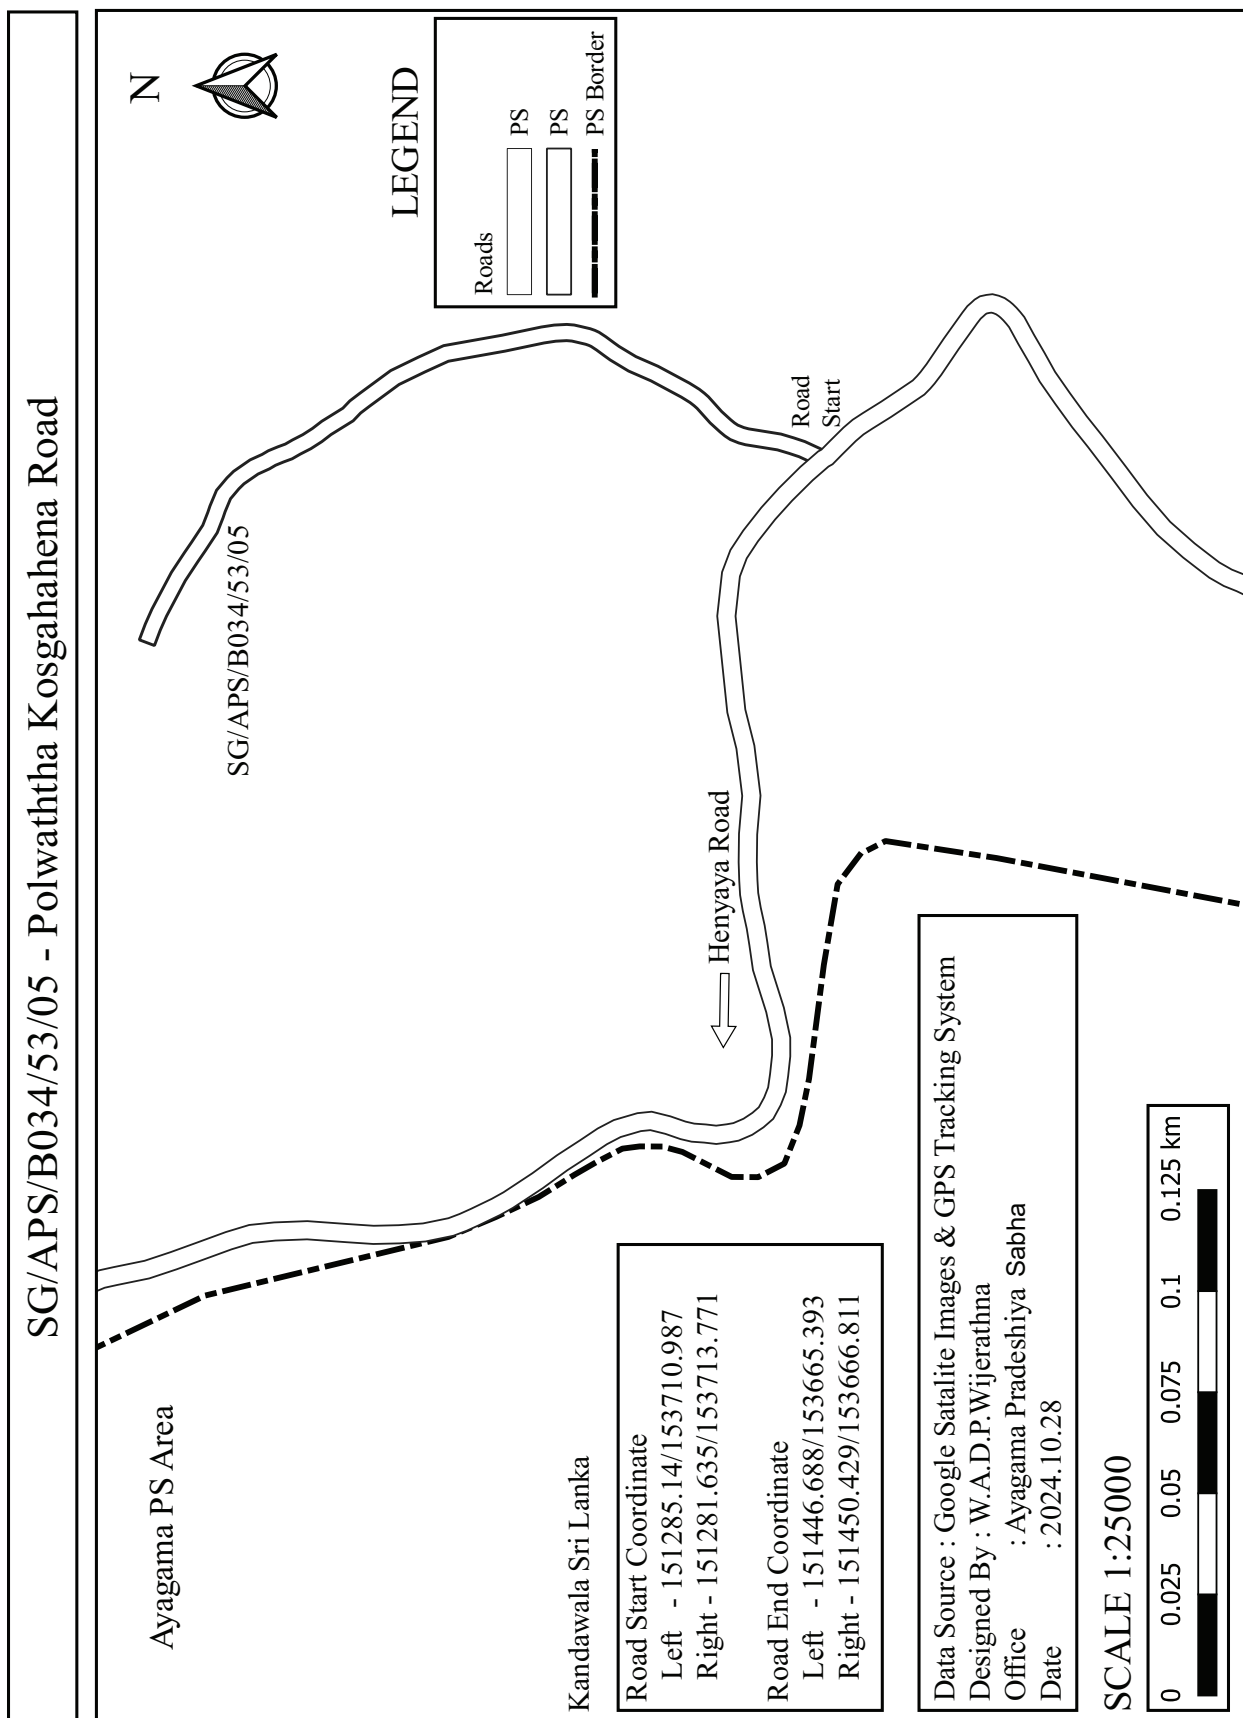


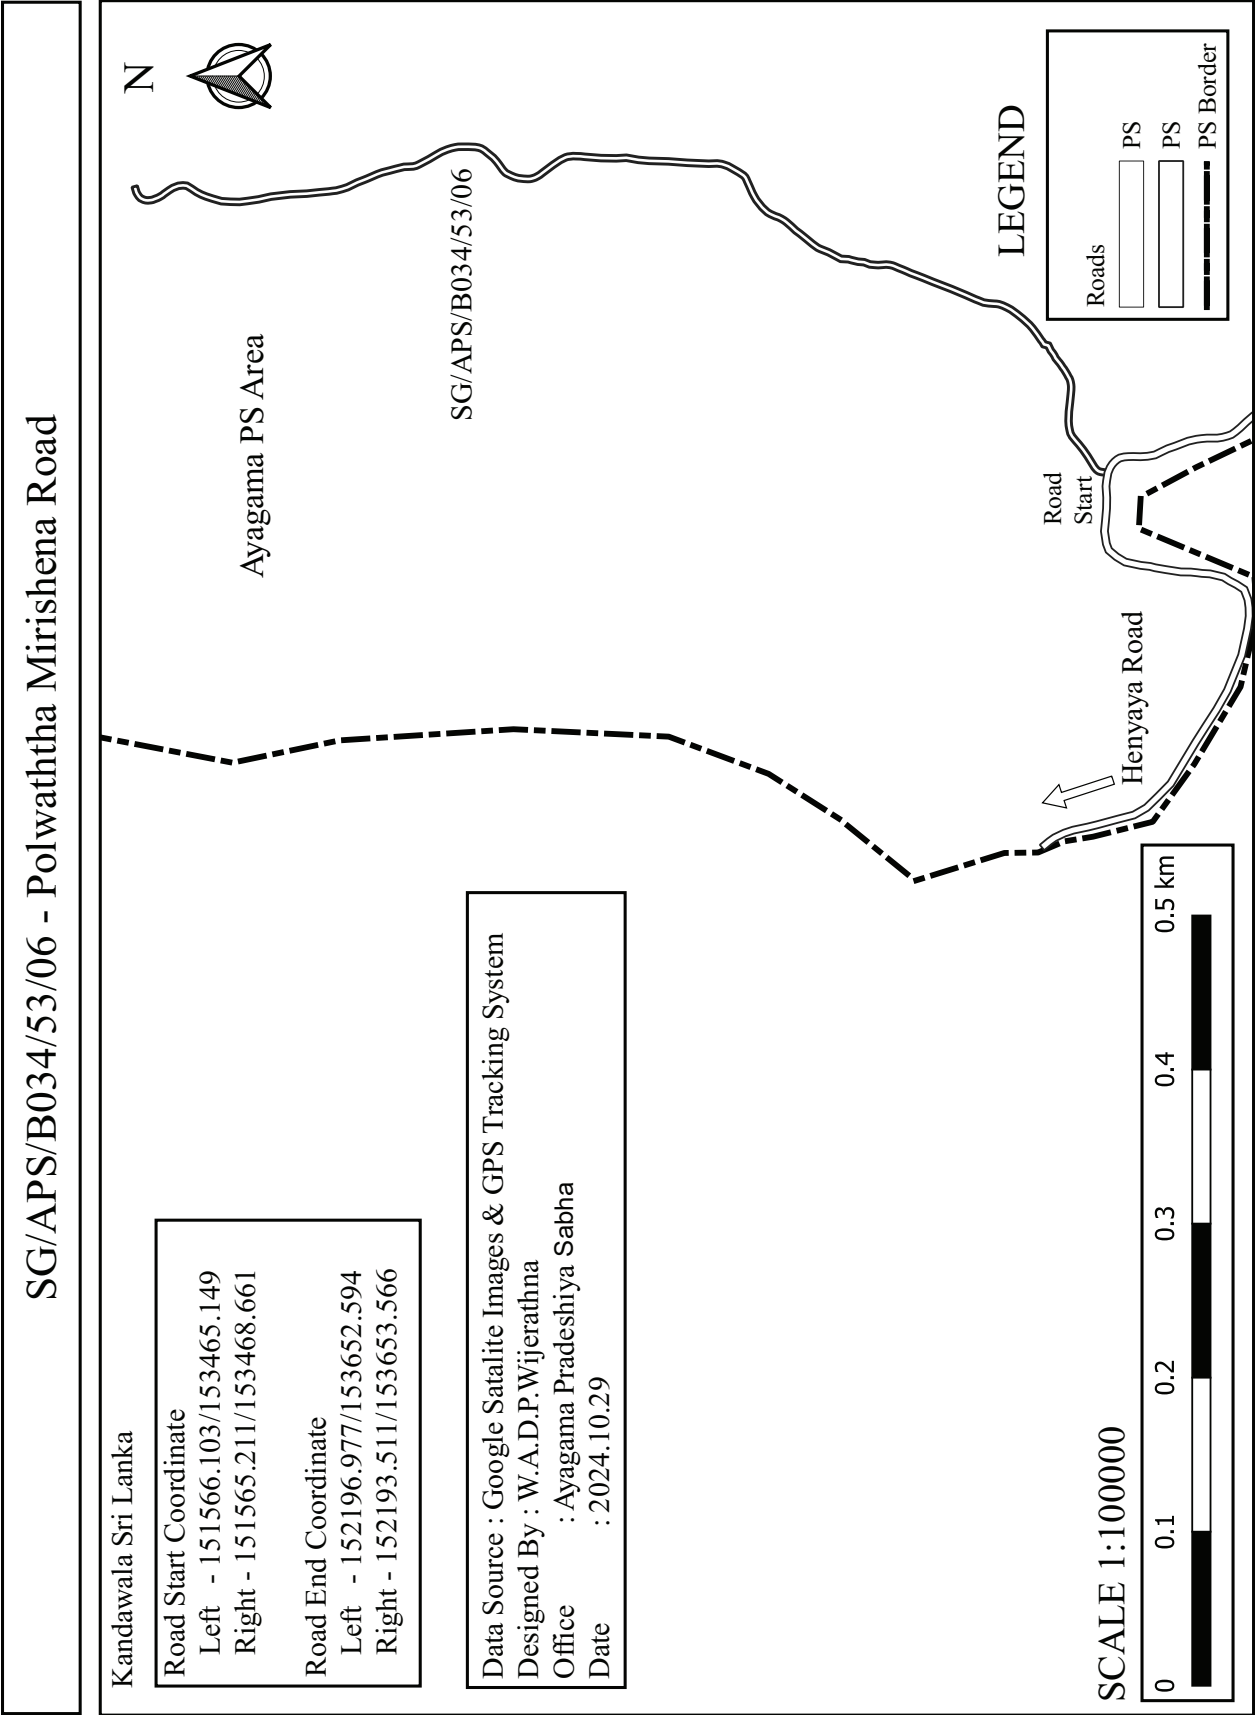

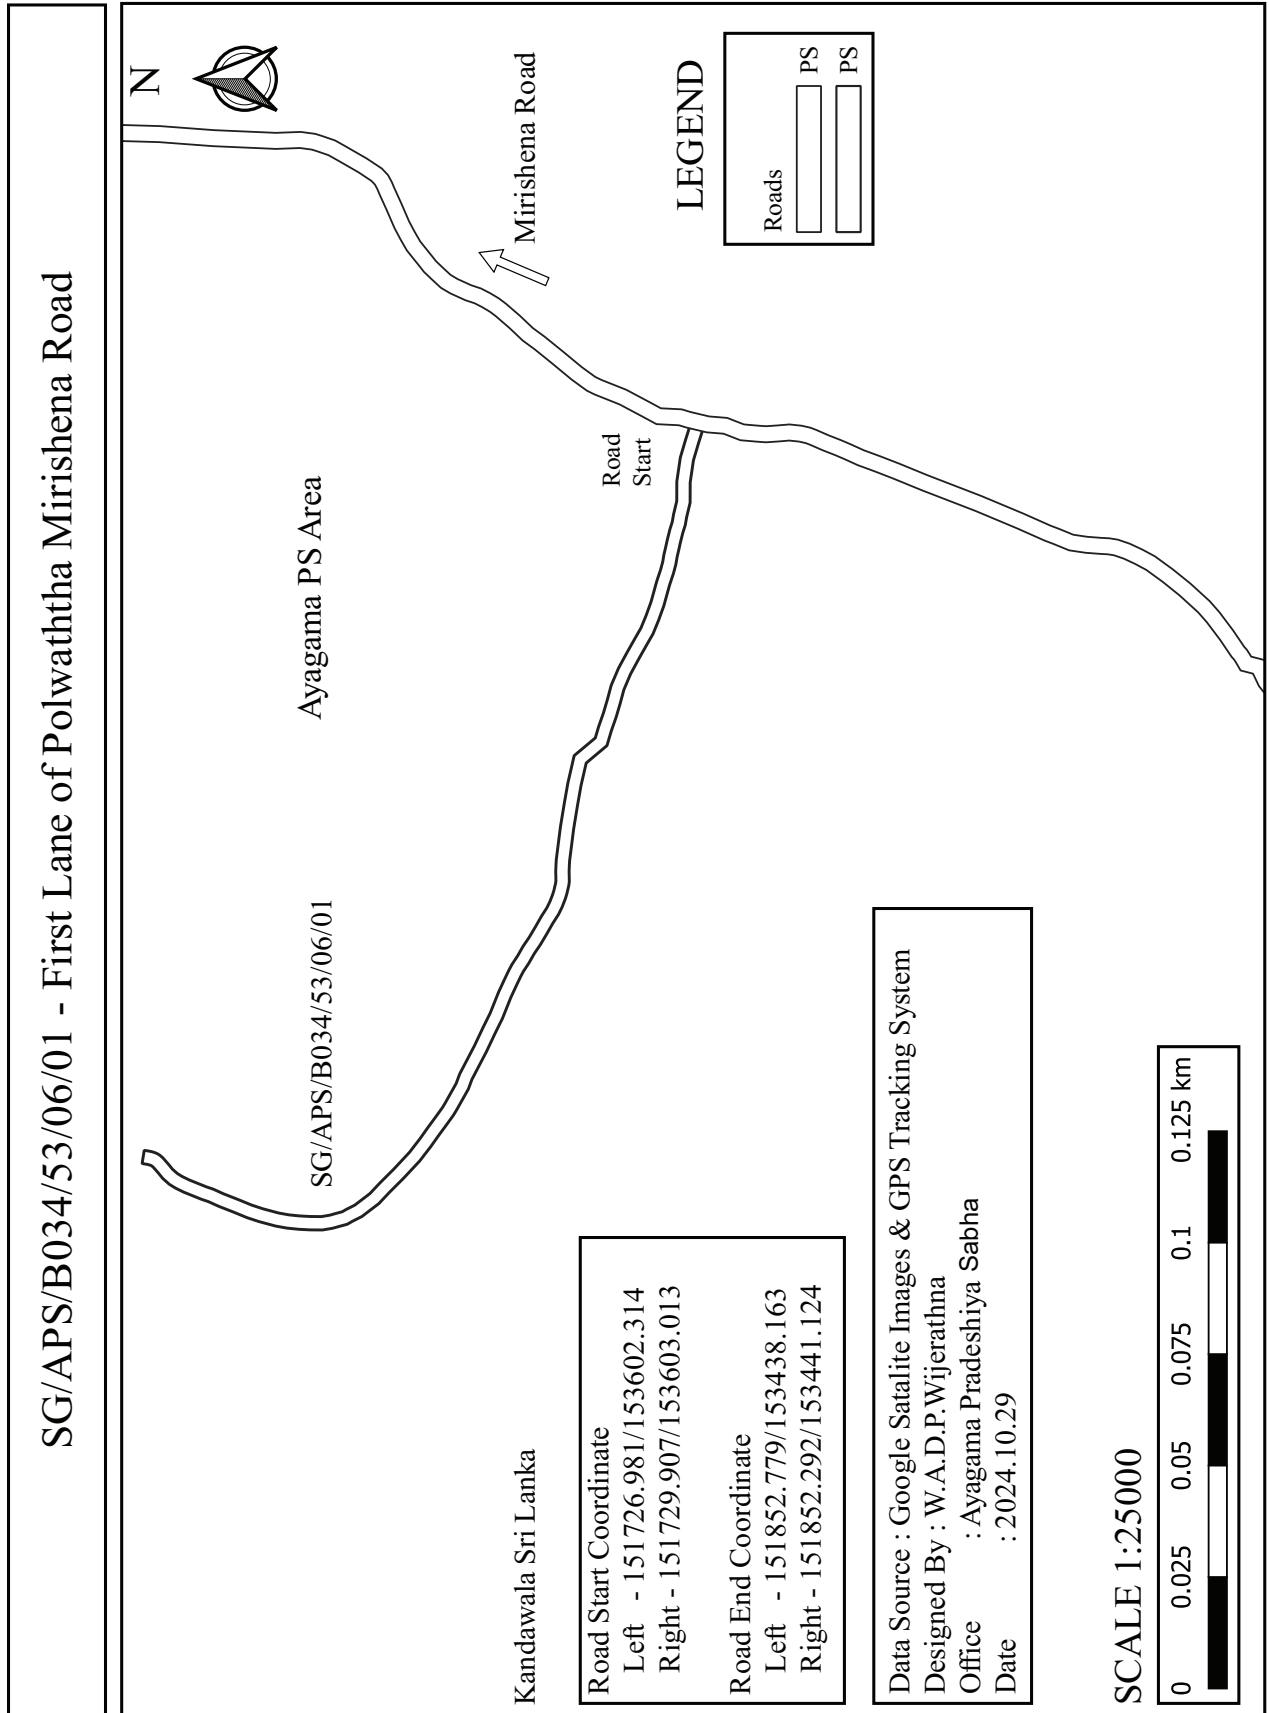


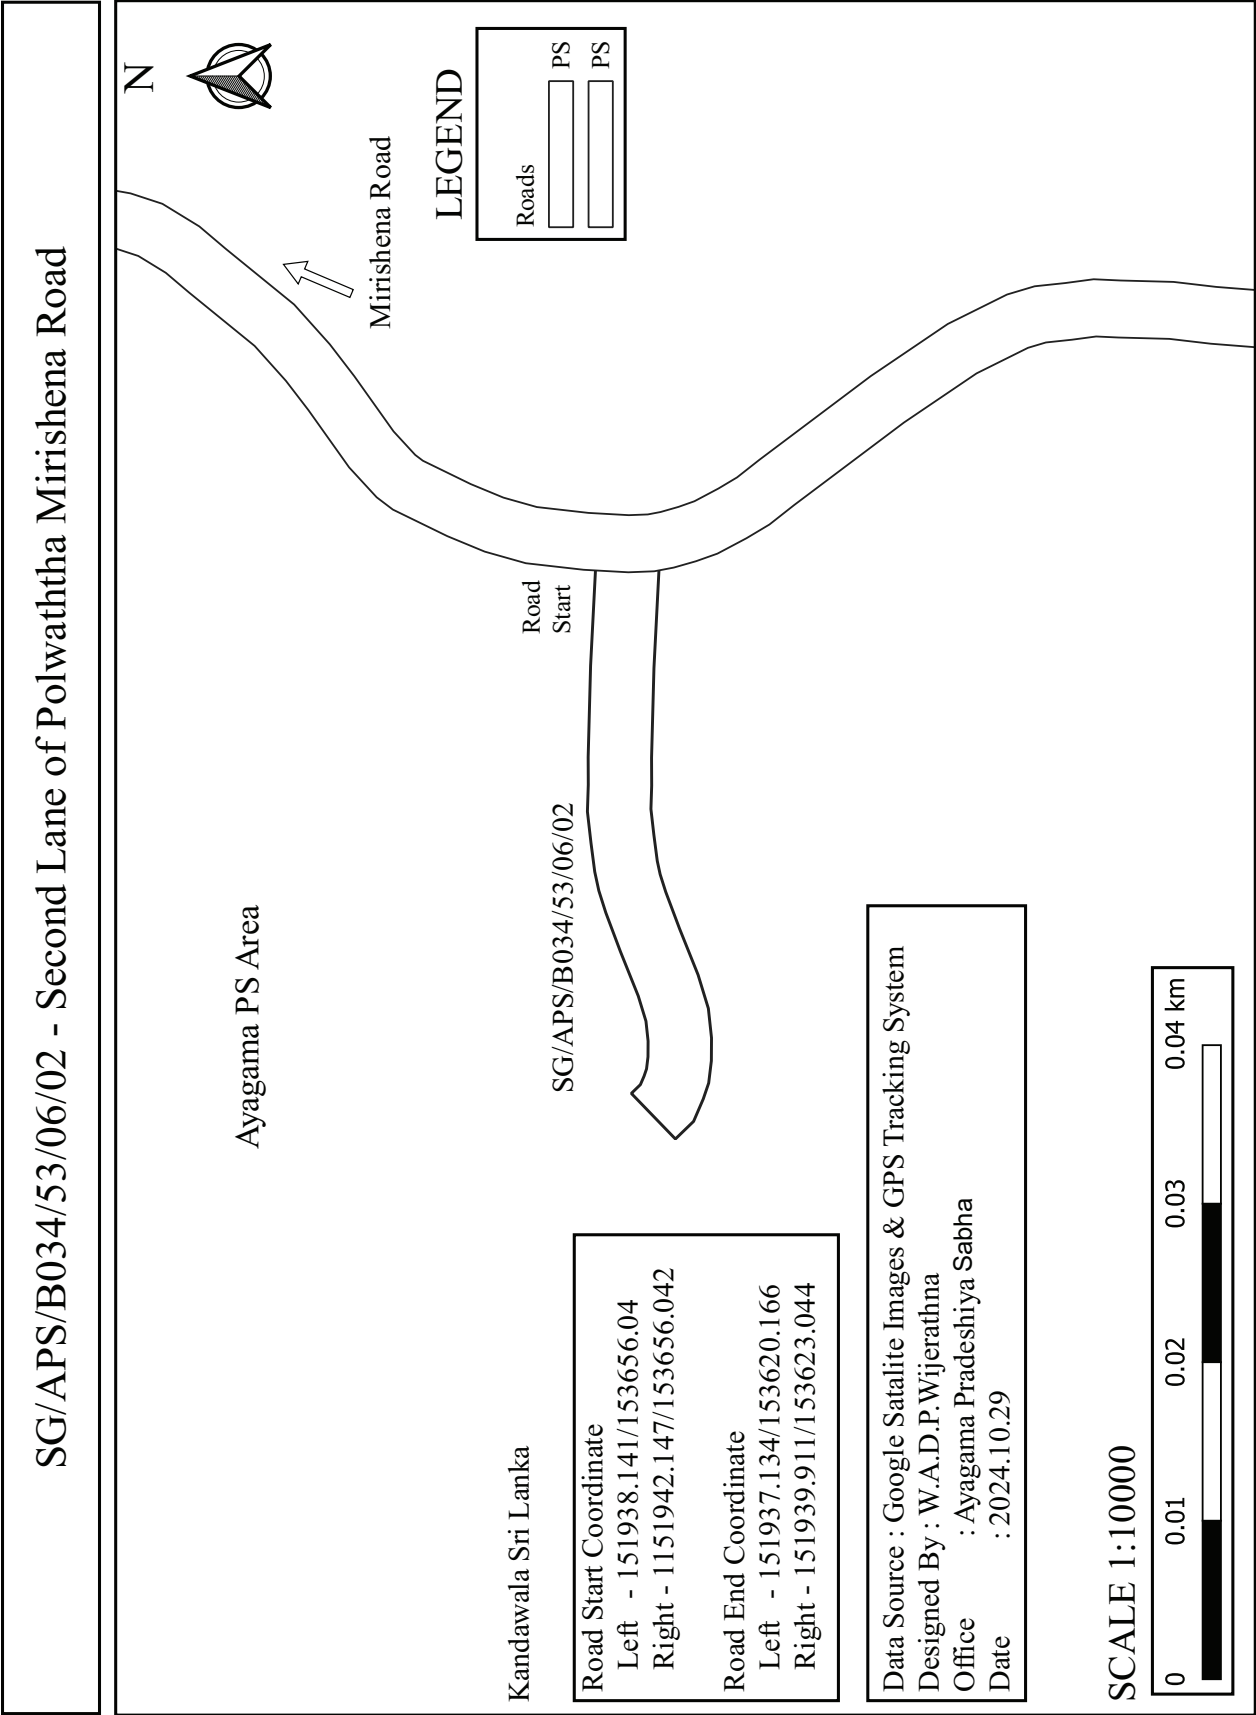

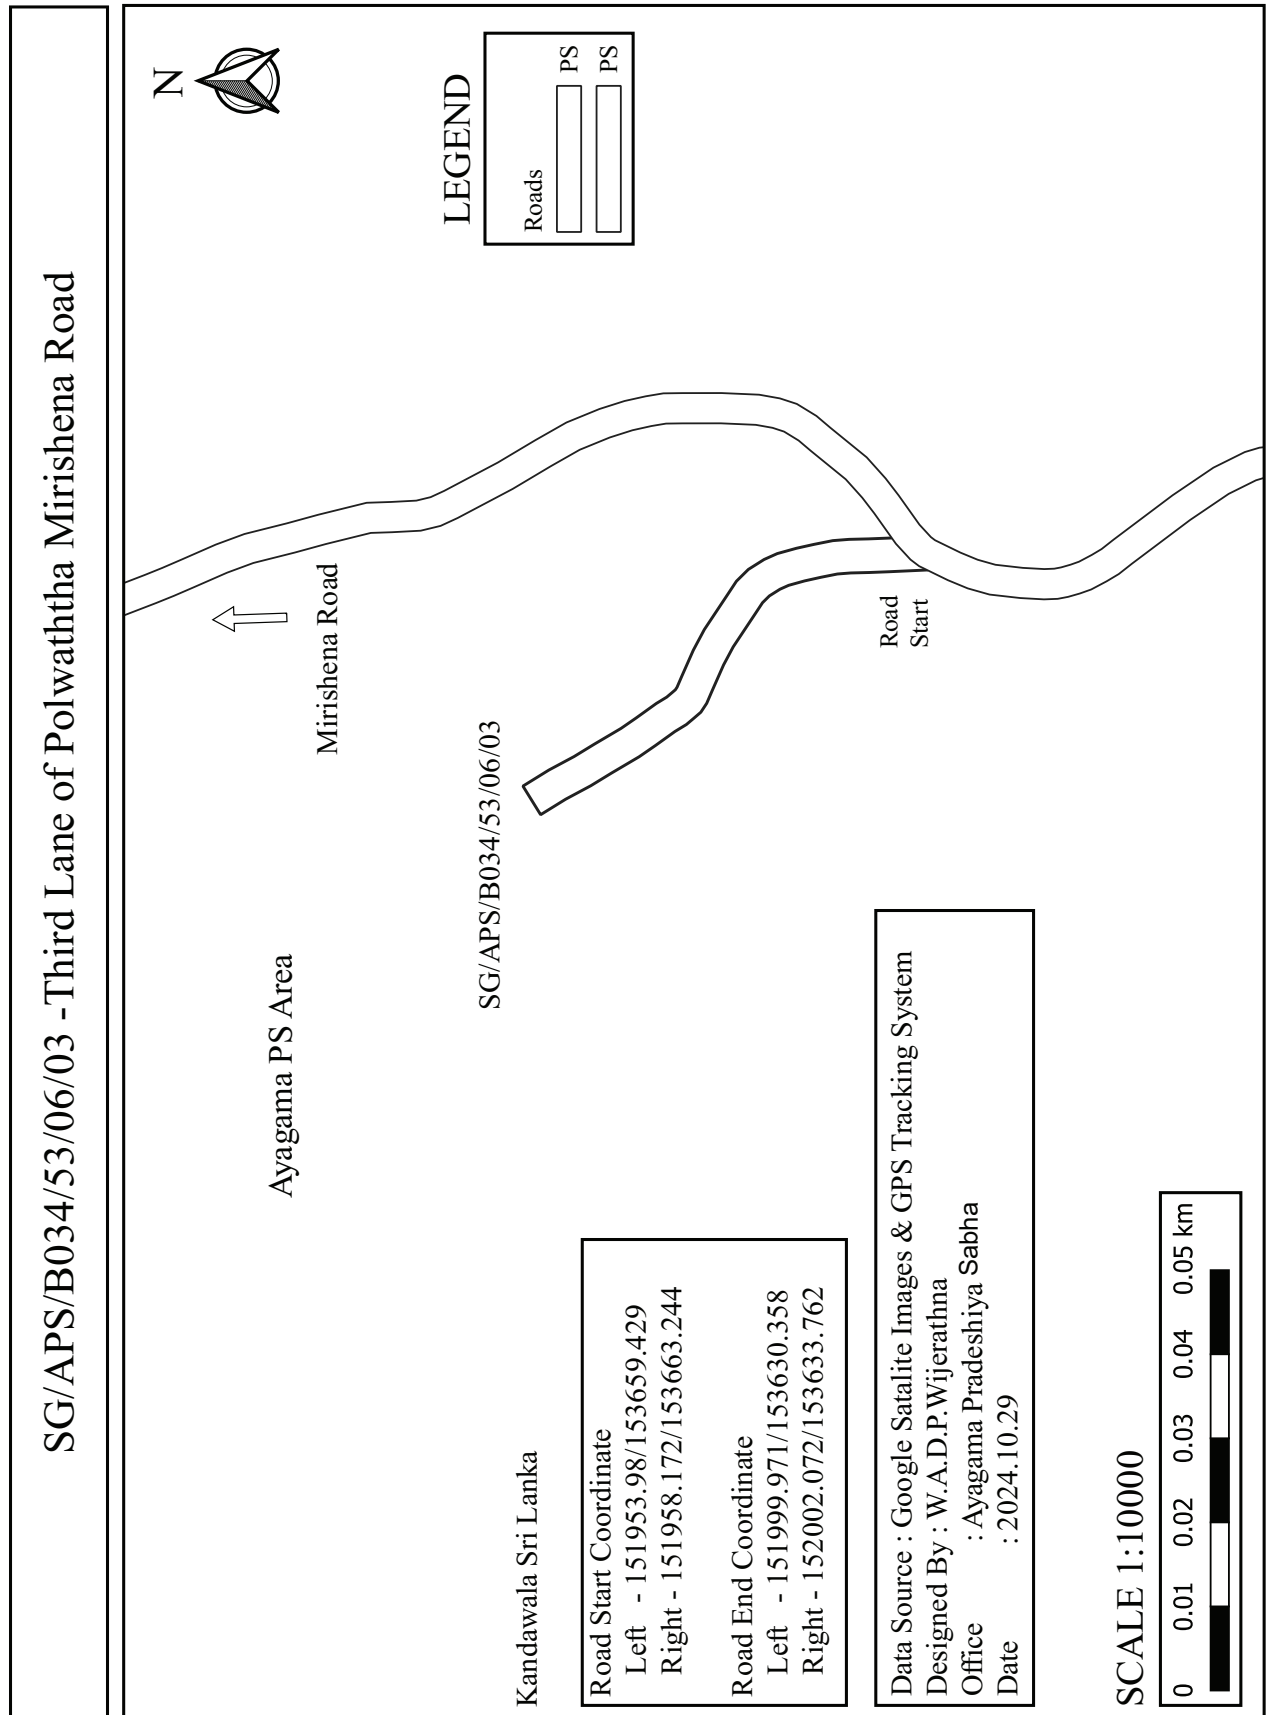


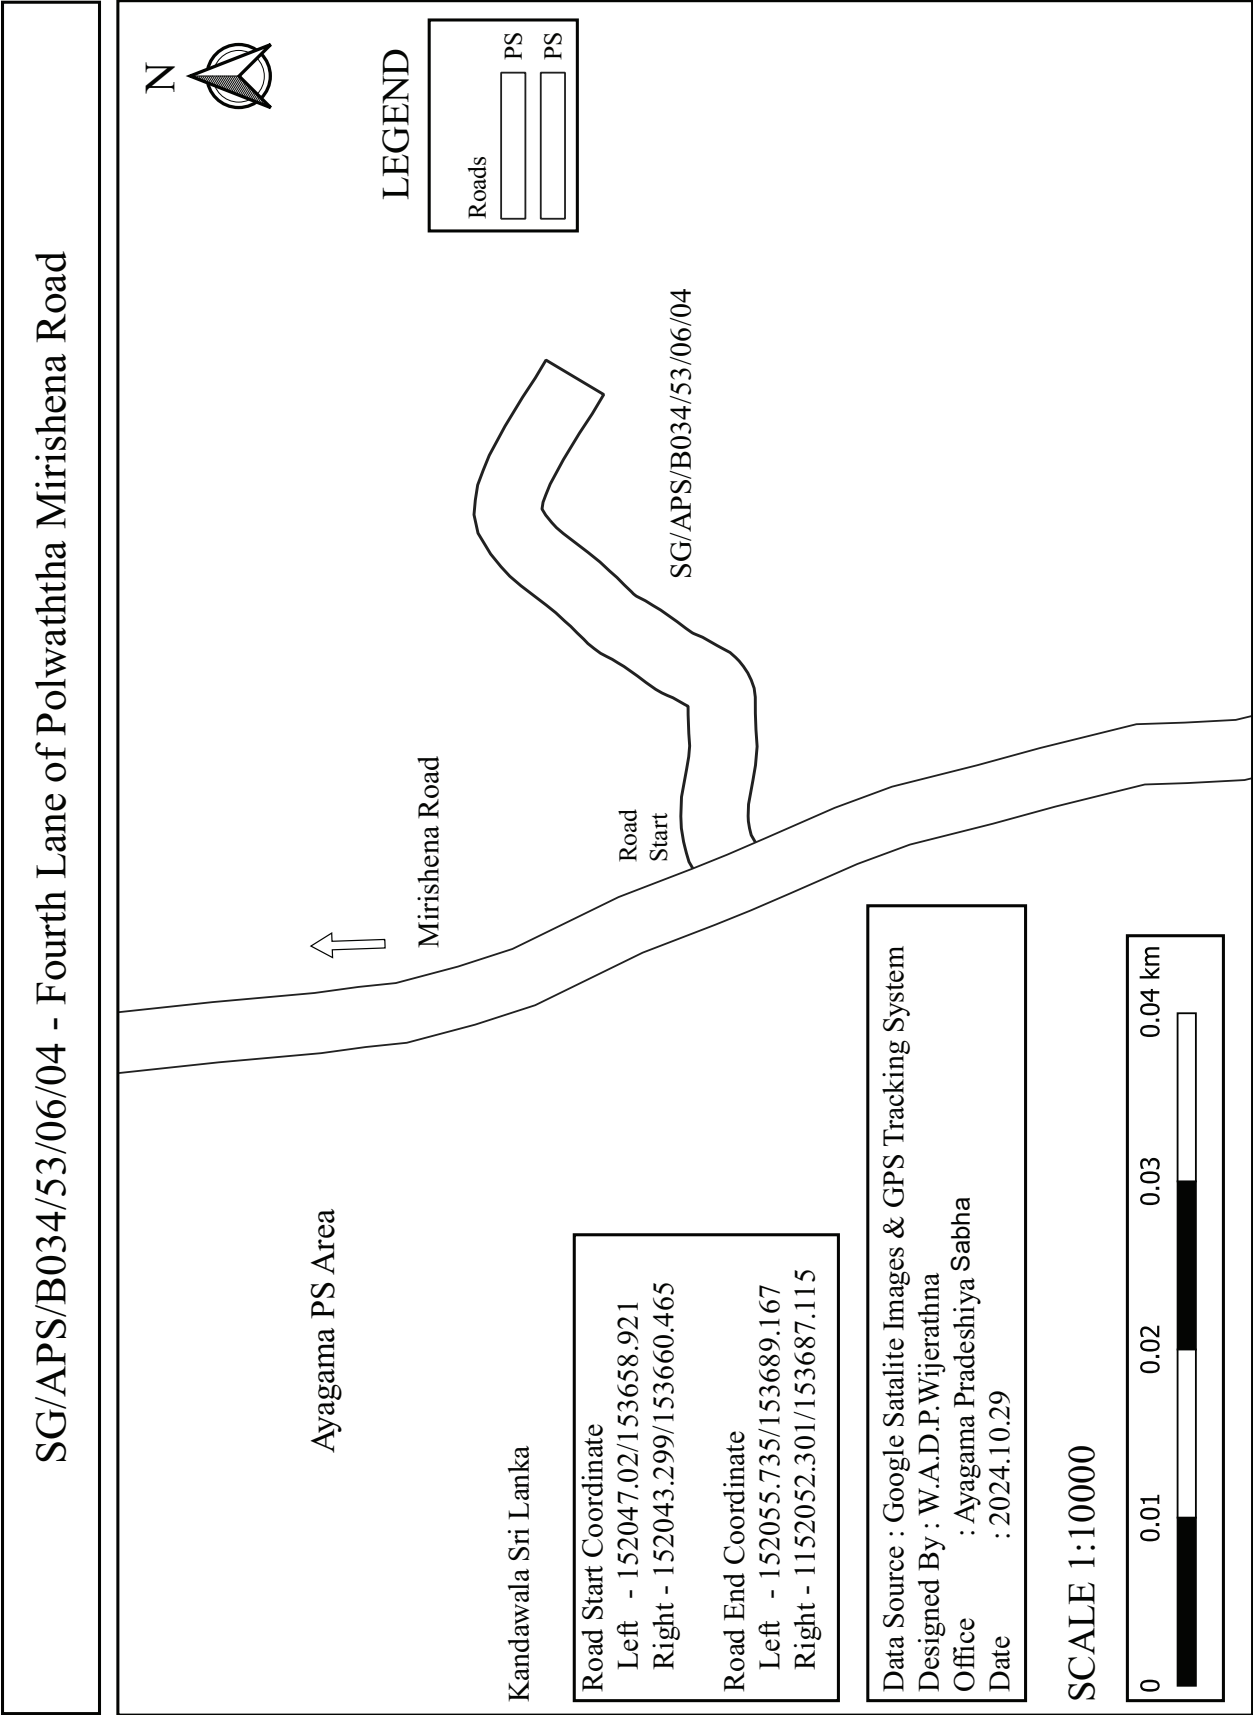

SG/APS/B034/53/07 - Polwaththa Temple Road

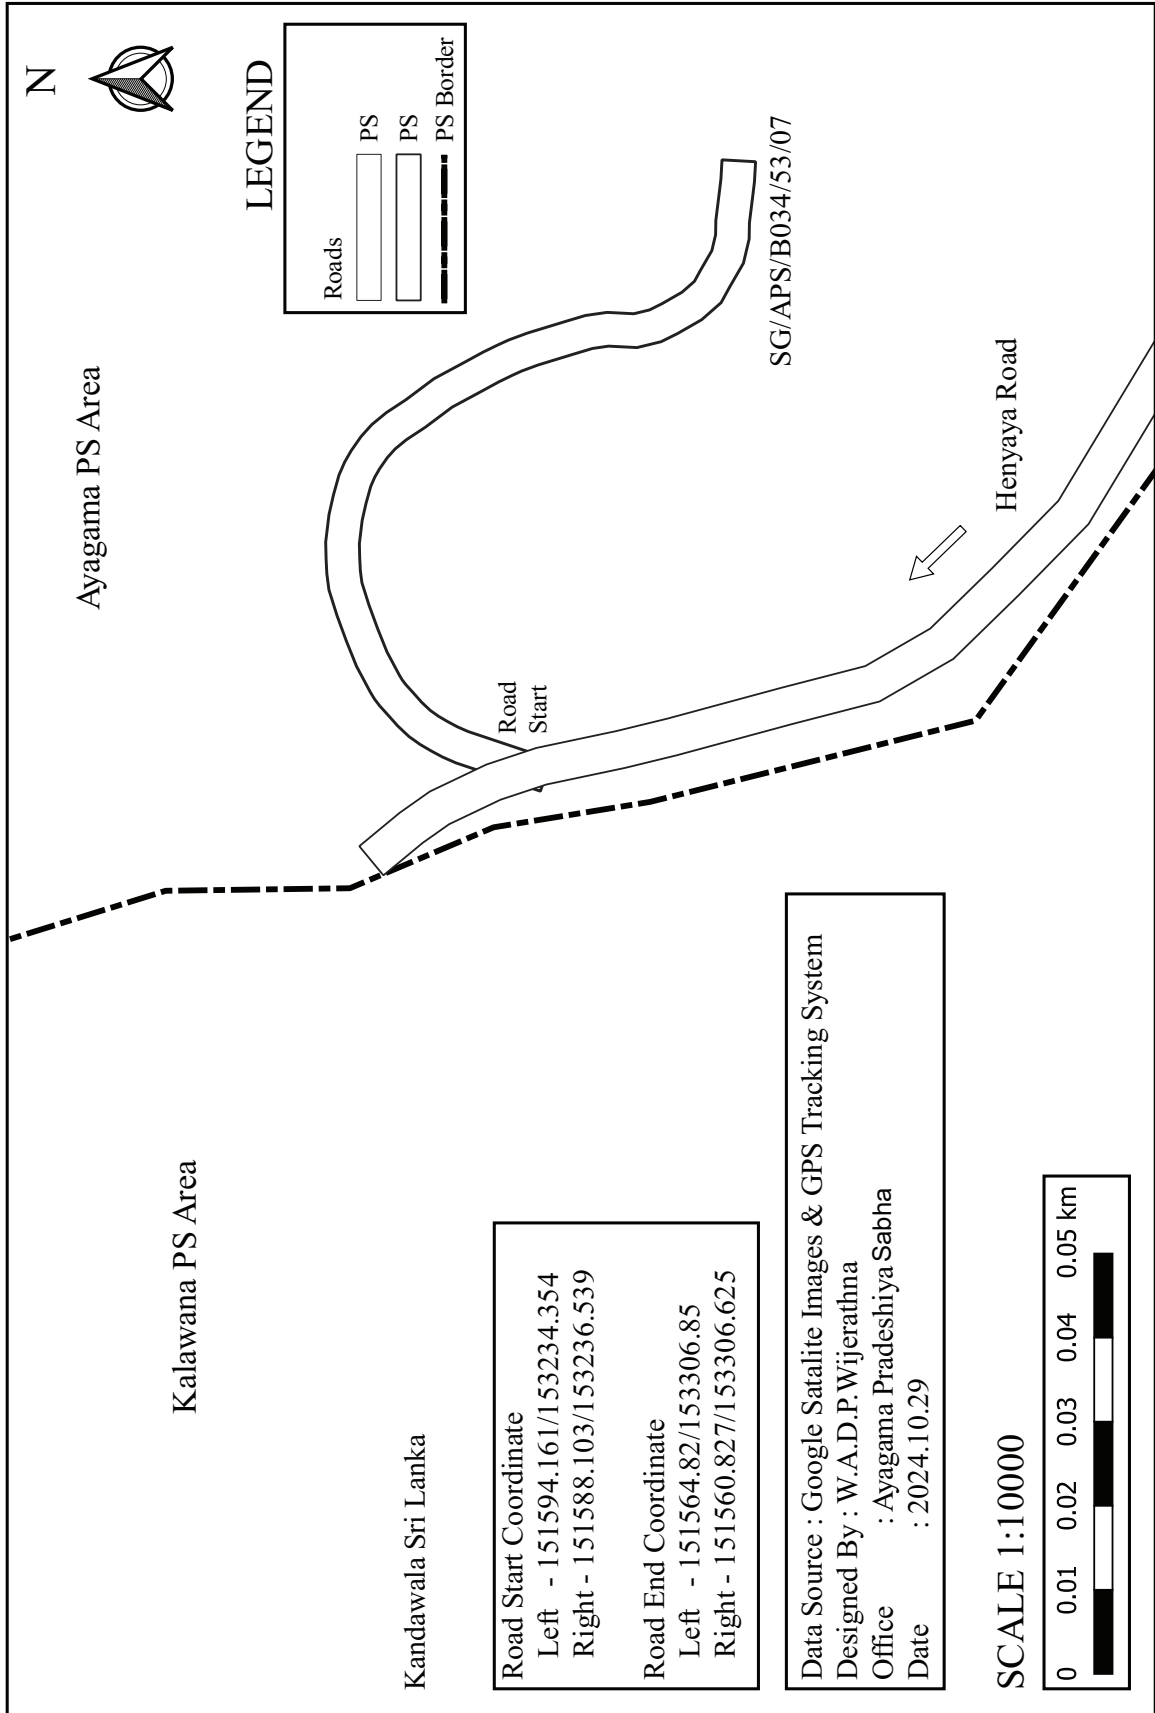

Kandawala Sri Lanka

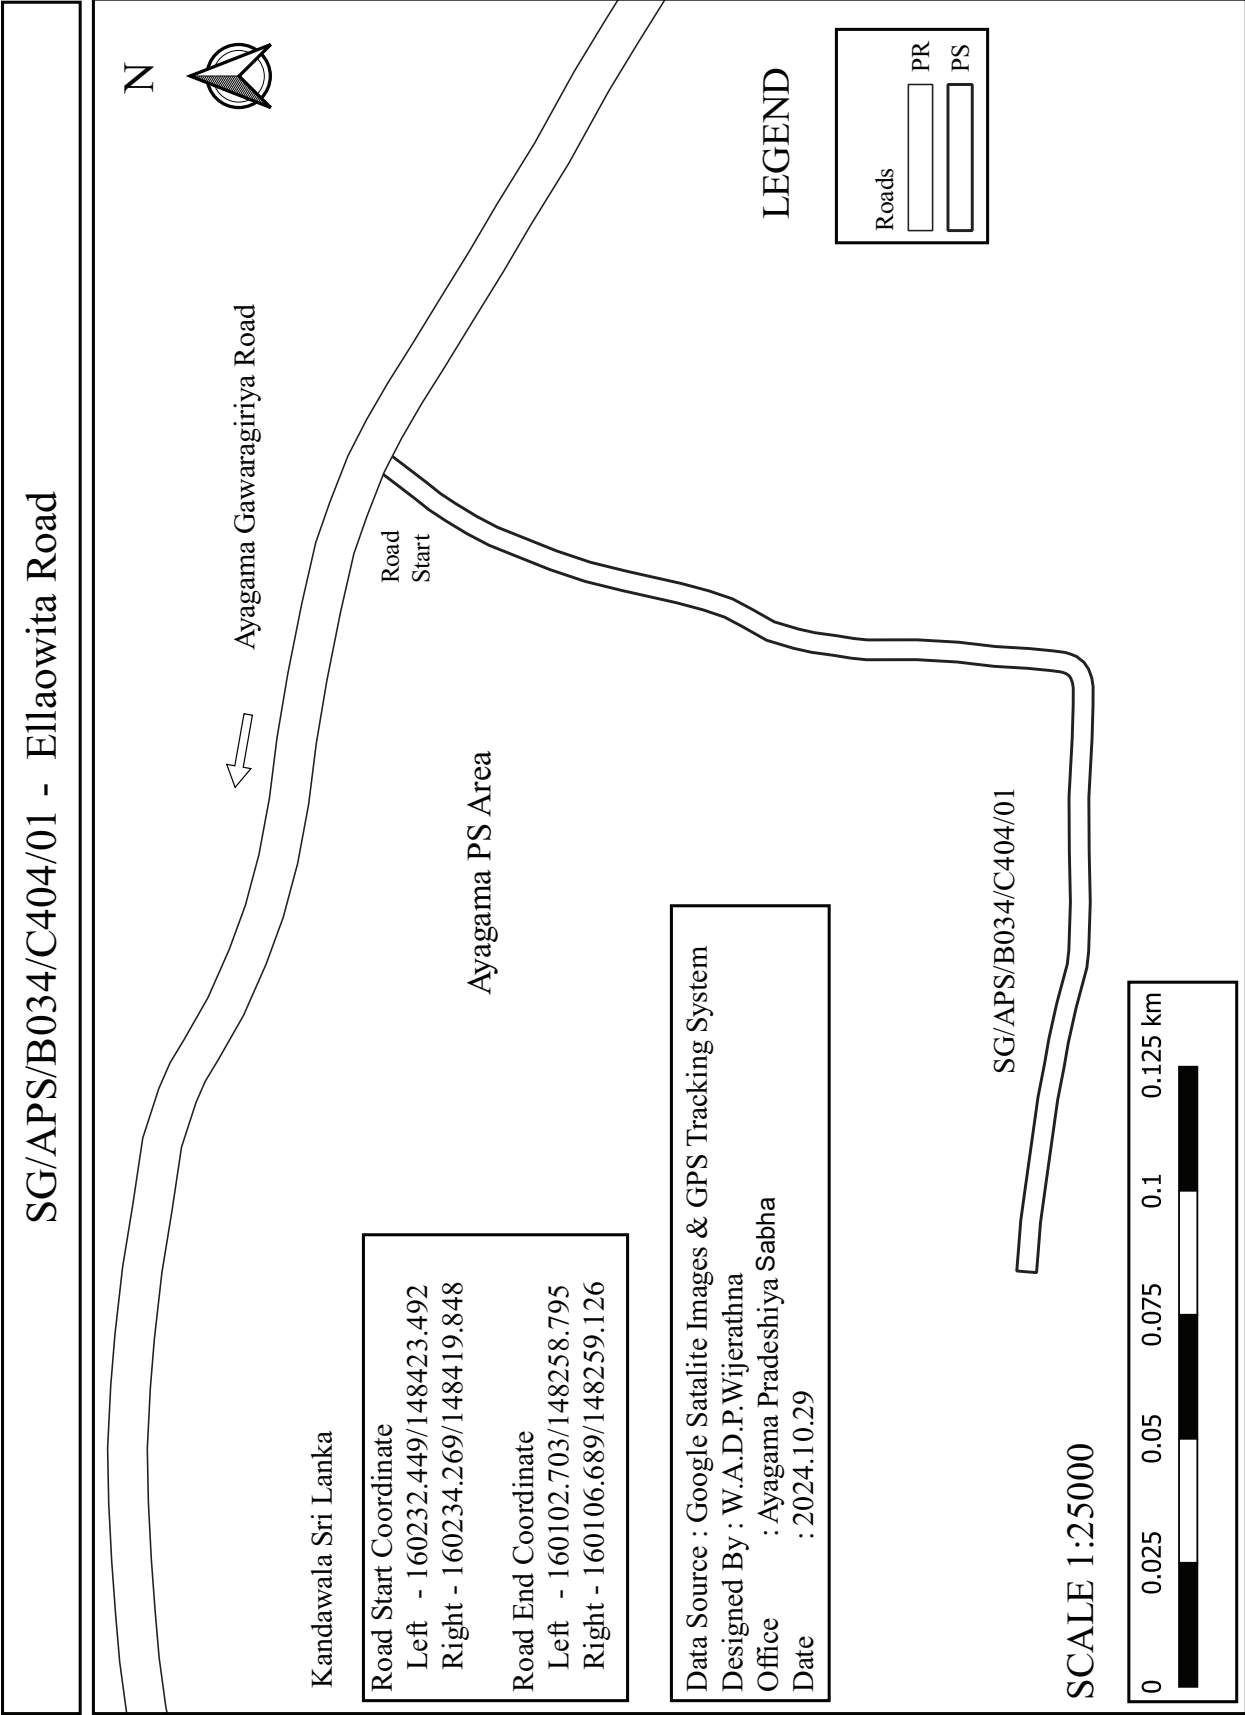

SG/APS/B034/C404/02 - Road Near Ayagama Pradeshiya Sabha



Kandawala Sri Lanka

Road Start Coordinate

Left - 160277.687/148300.551

Right - 160275.962/148303.6

Road End Coordinate

Left - 1160360.472/148318.25

Right - 160361.682/148321.535

Ayagama PS Area

SG/APS/B034/C404/02

LEGEND

Roads

PR

PS

Data Source : Google Satalite Images & GPS Tracking System

Designed By : W.A.D.P.Wijerathna

Office : Ayagama Pradeshiya Sabha

Date : 2024.10.29


← Ayagama Gawaragiriya Road


Road
Start


SCALE 1:10000

0 0.01 0.02 0.03 0.04 0.05 km




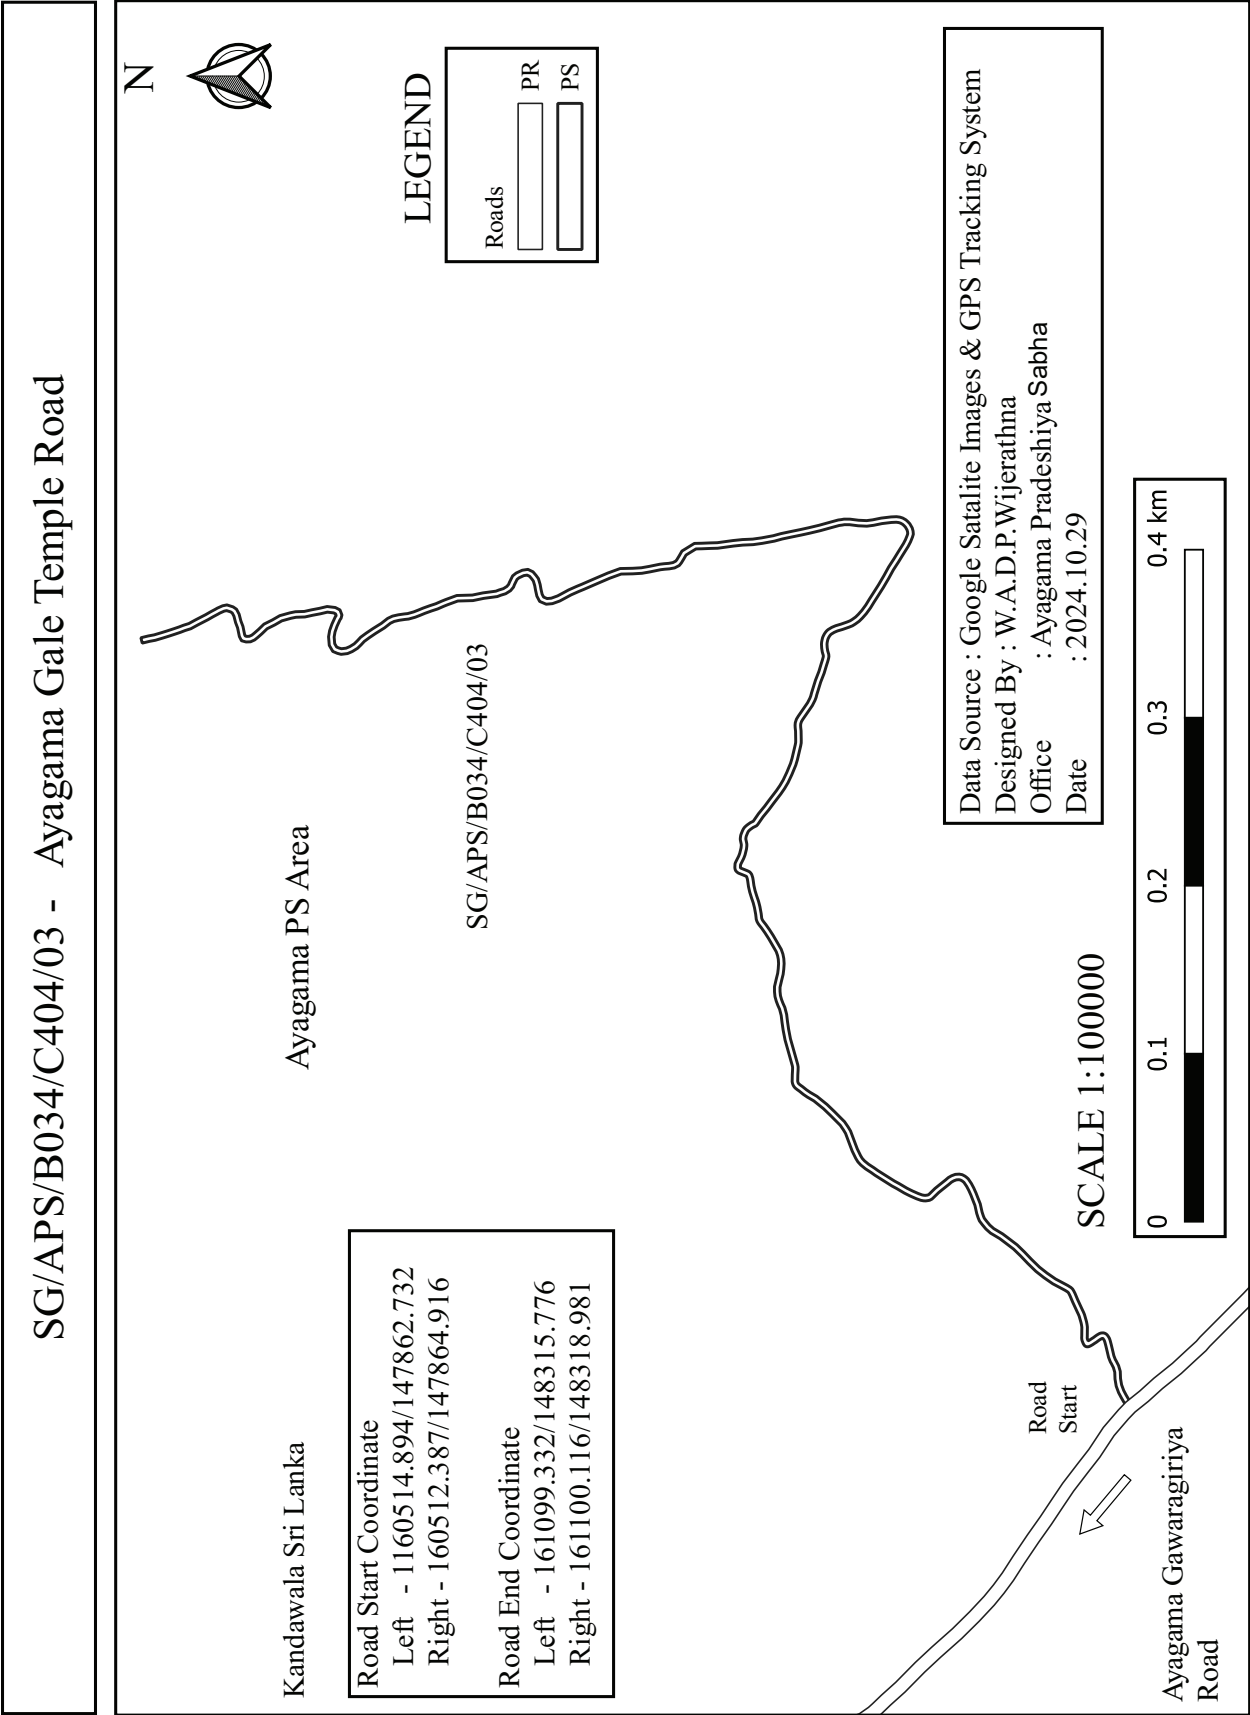


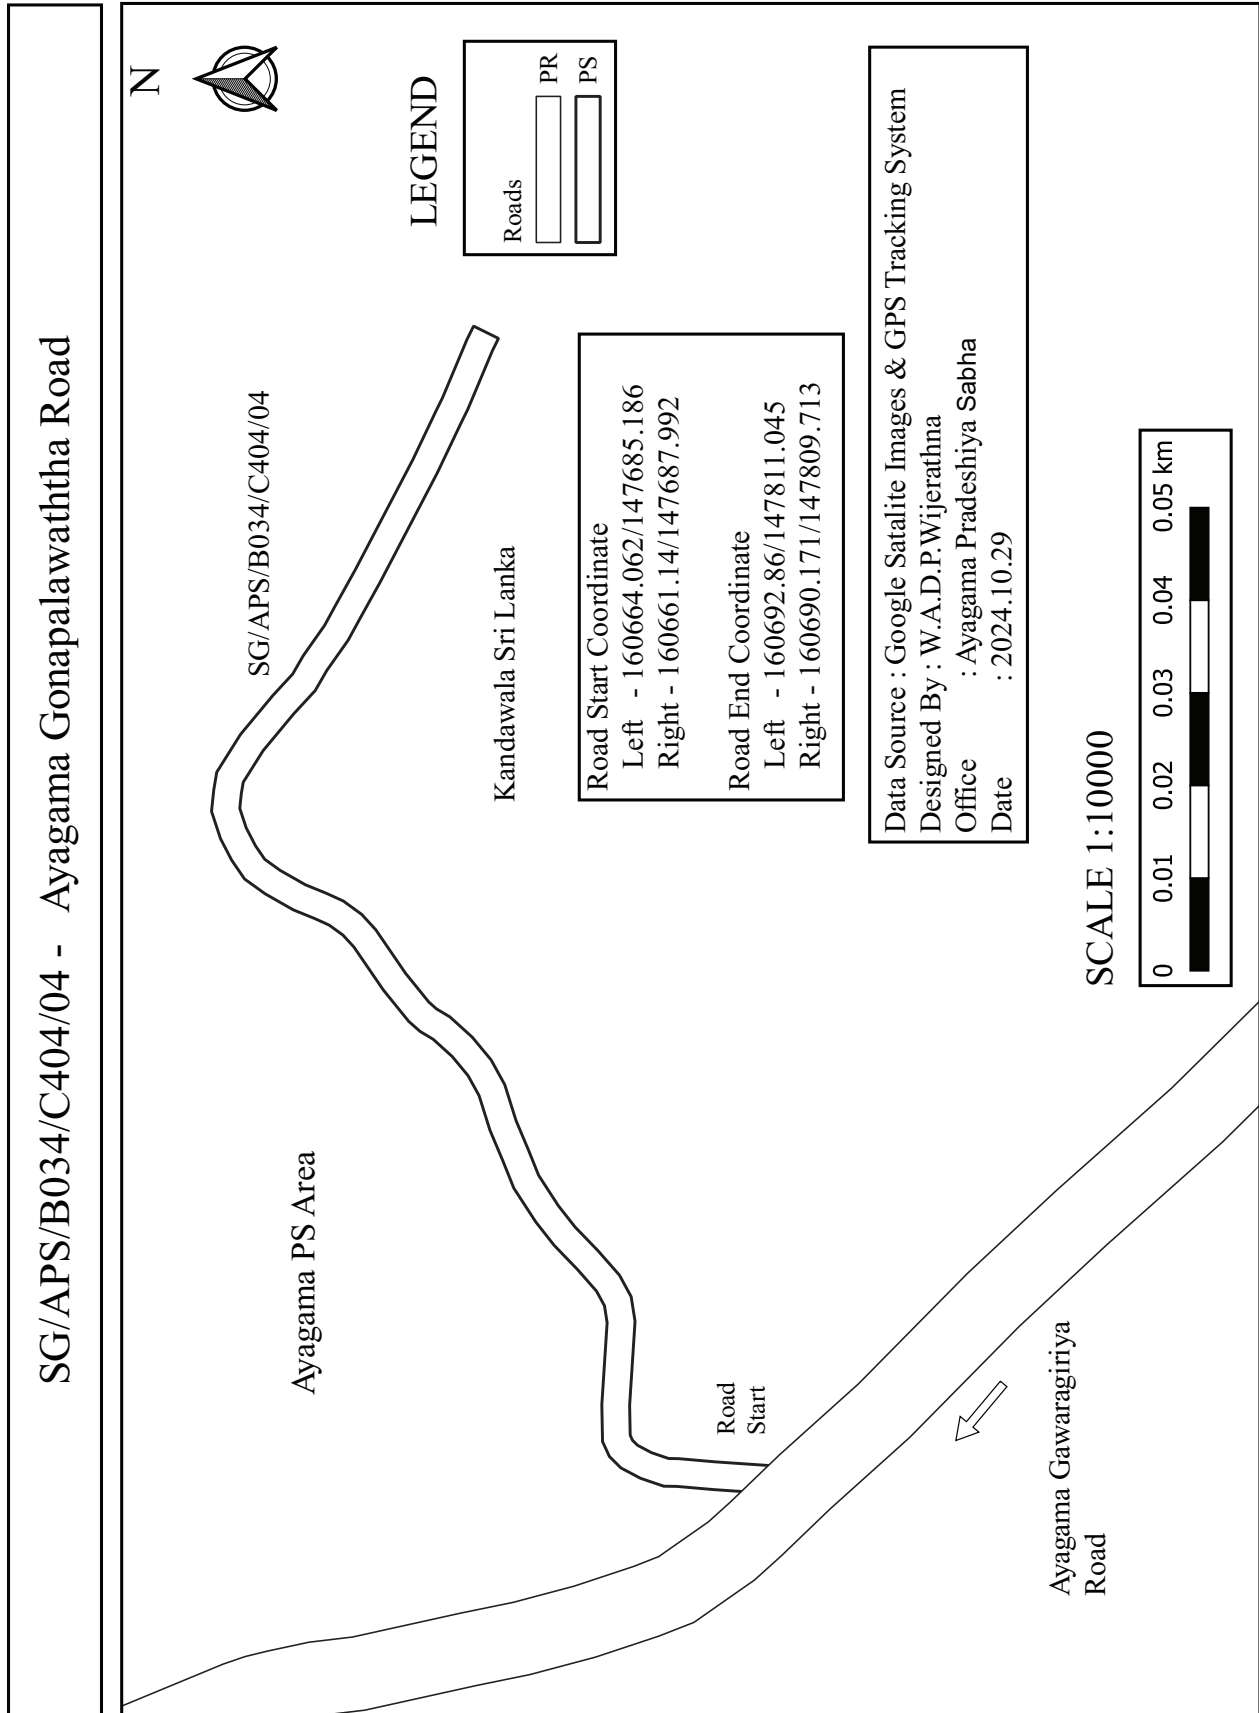


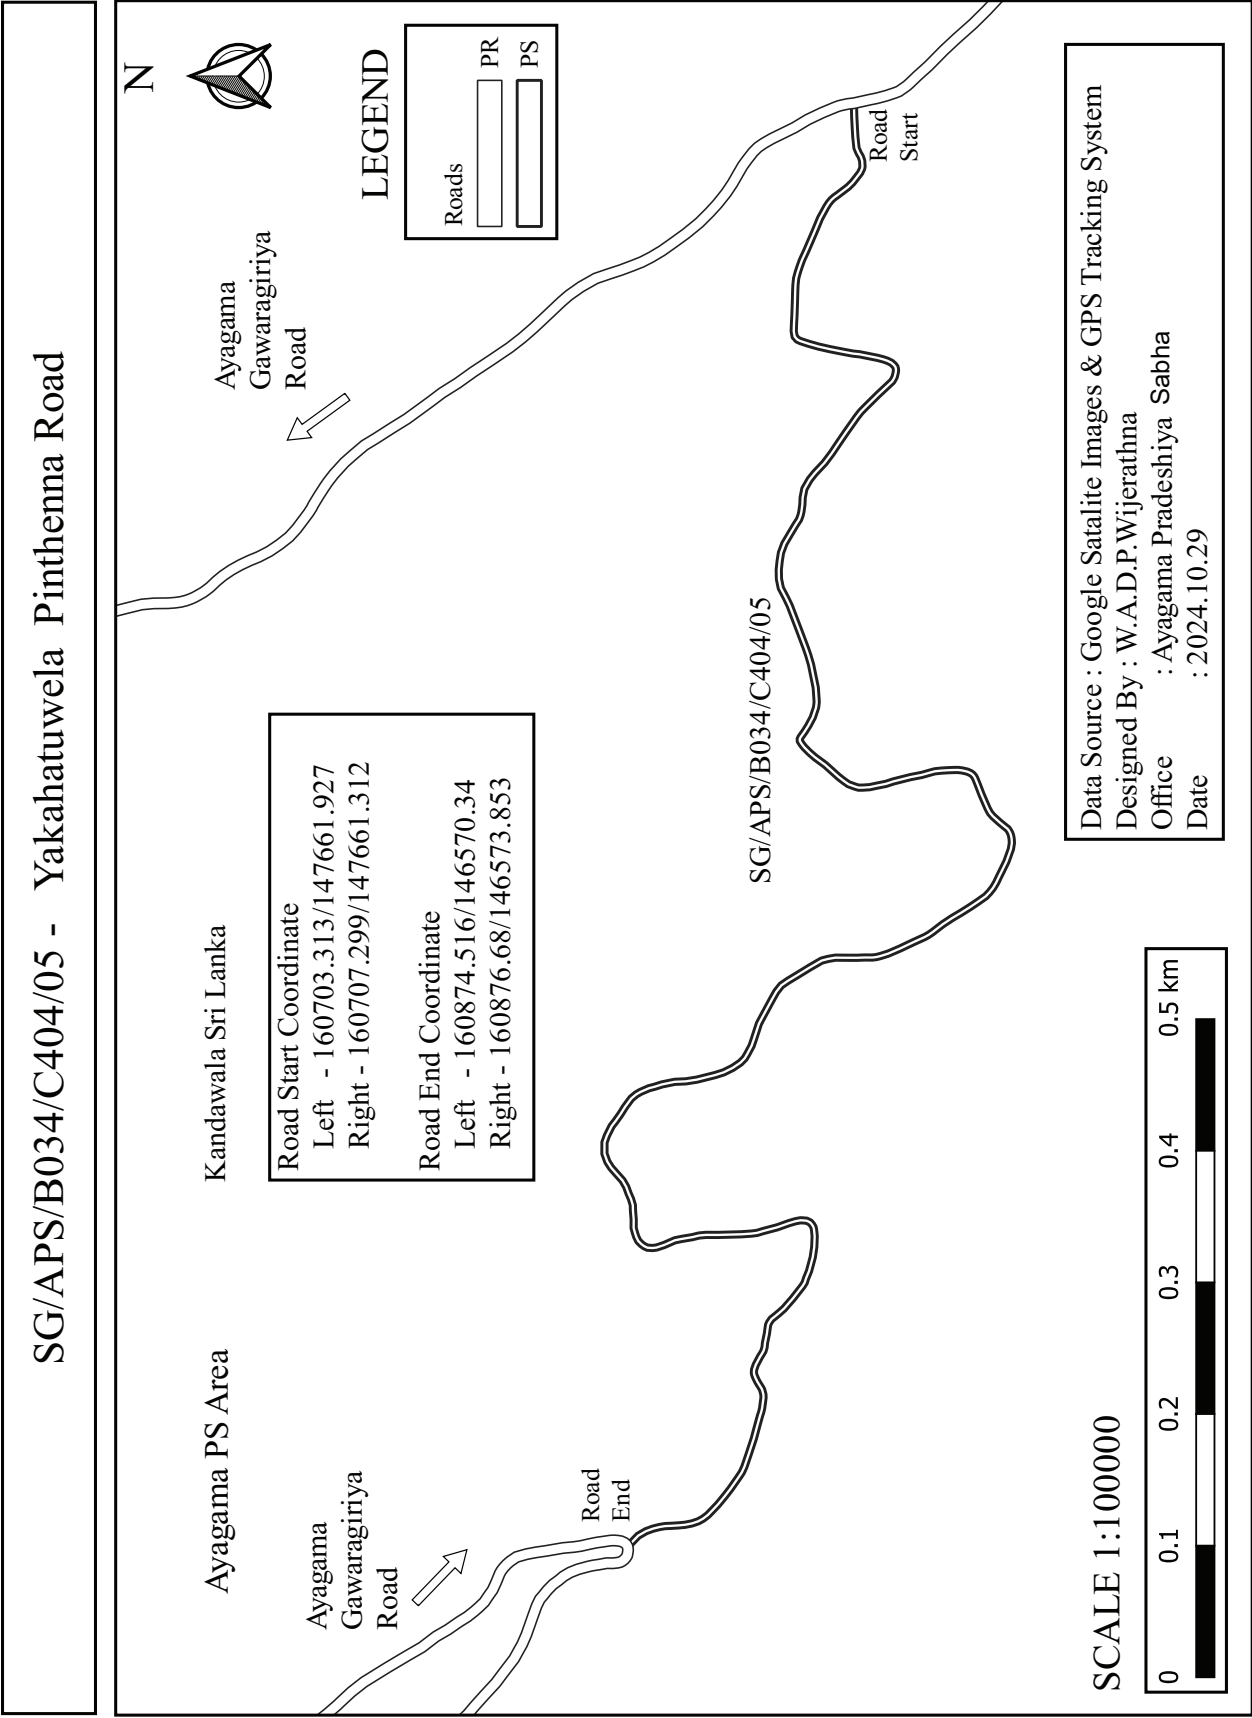


SG/APS/B034/C404/05/01 - Witowita Road

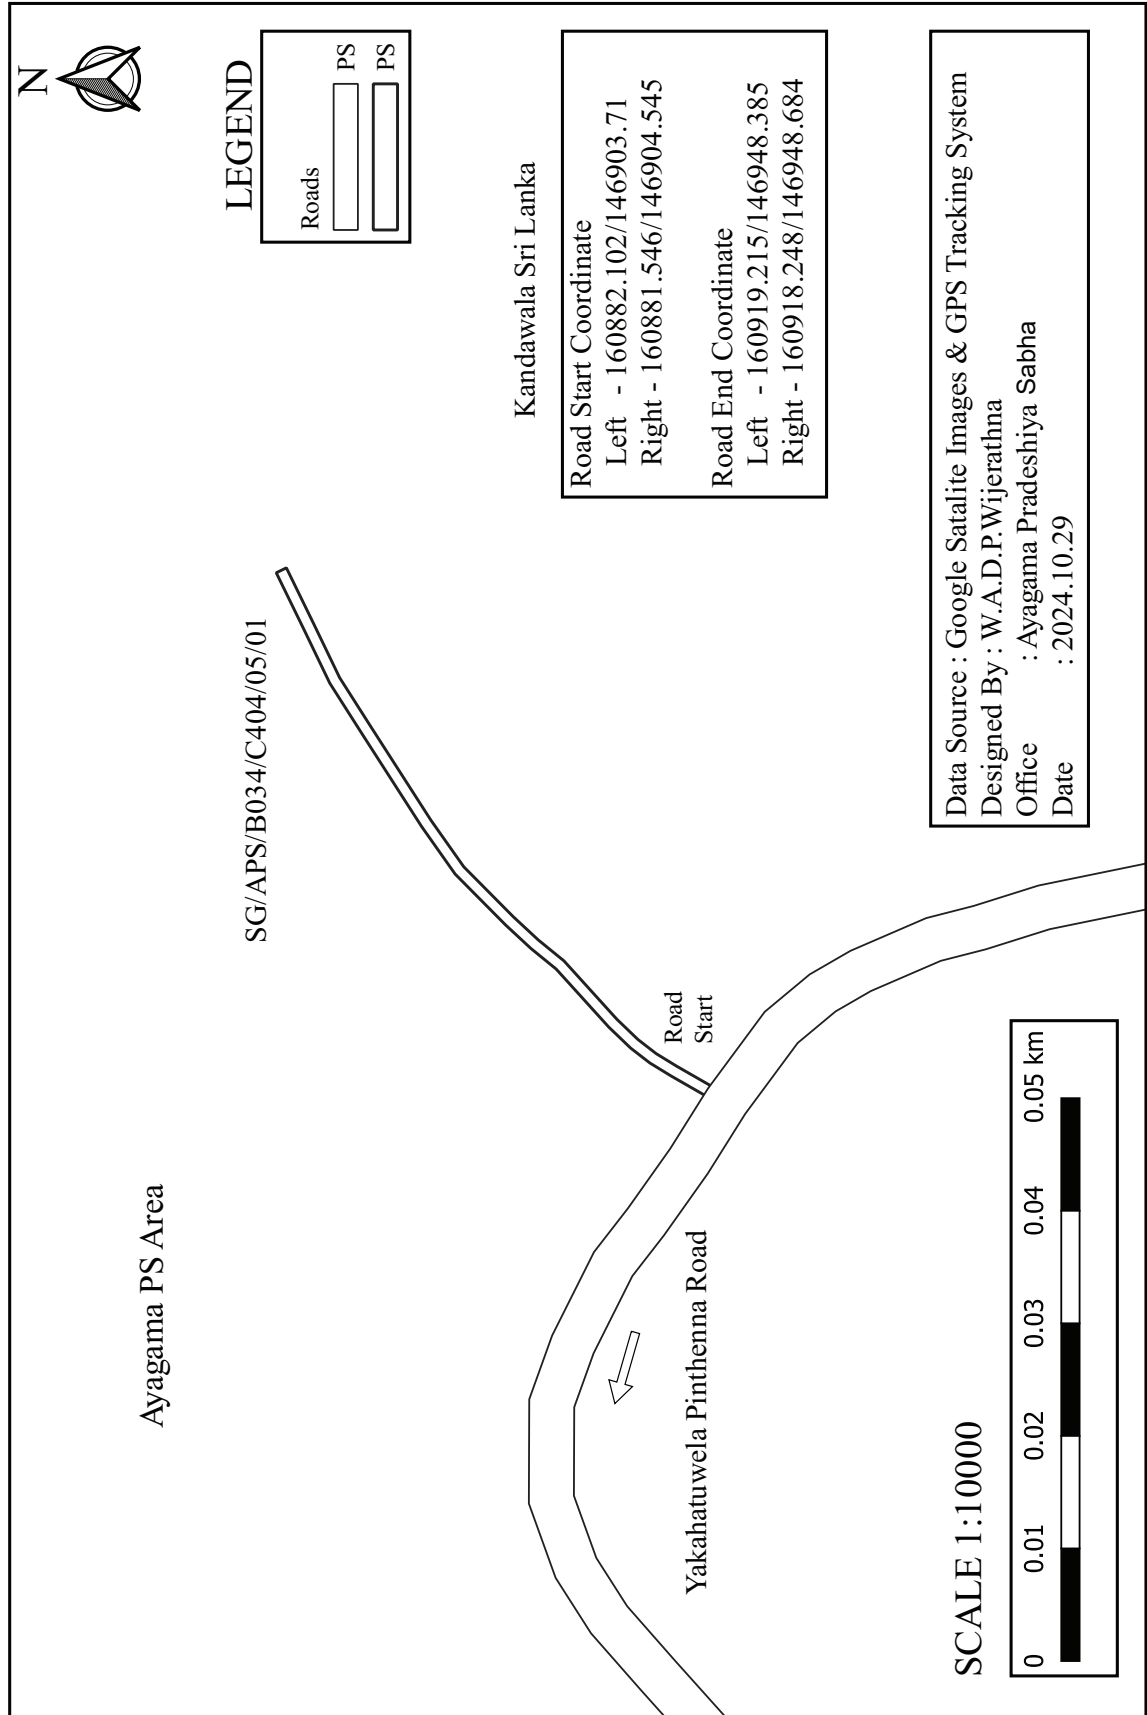


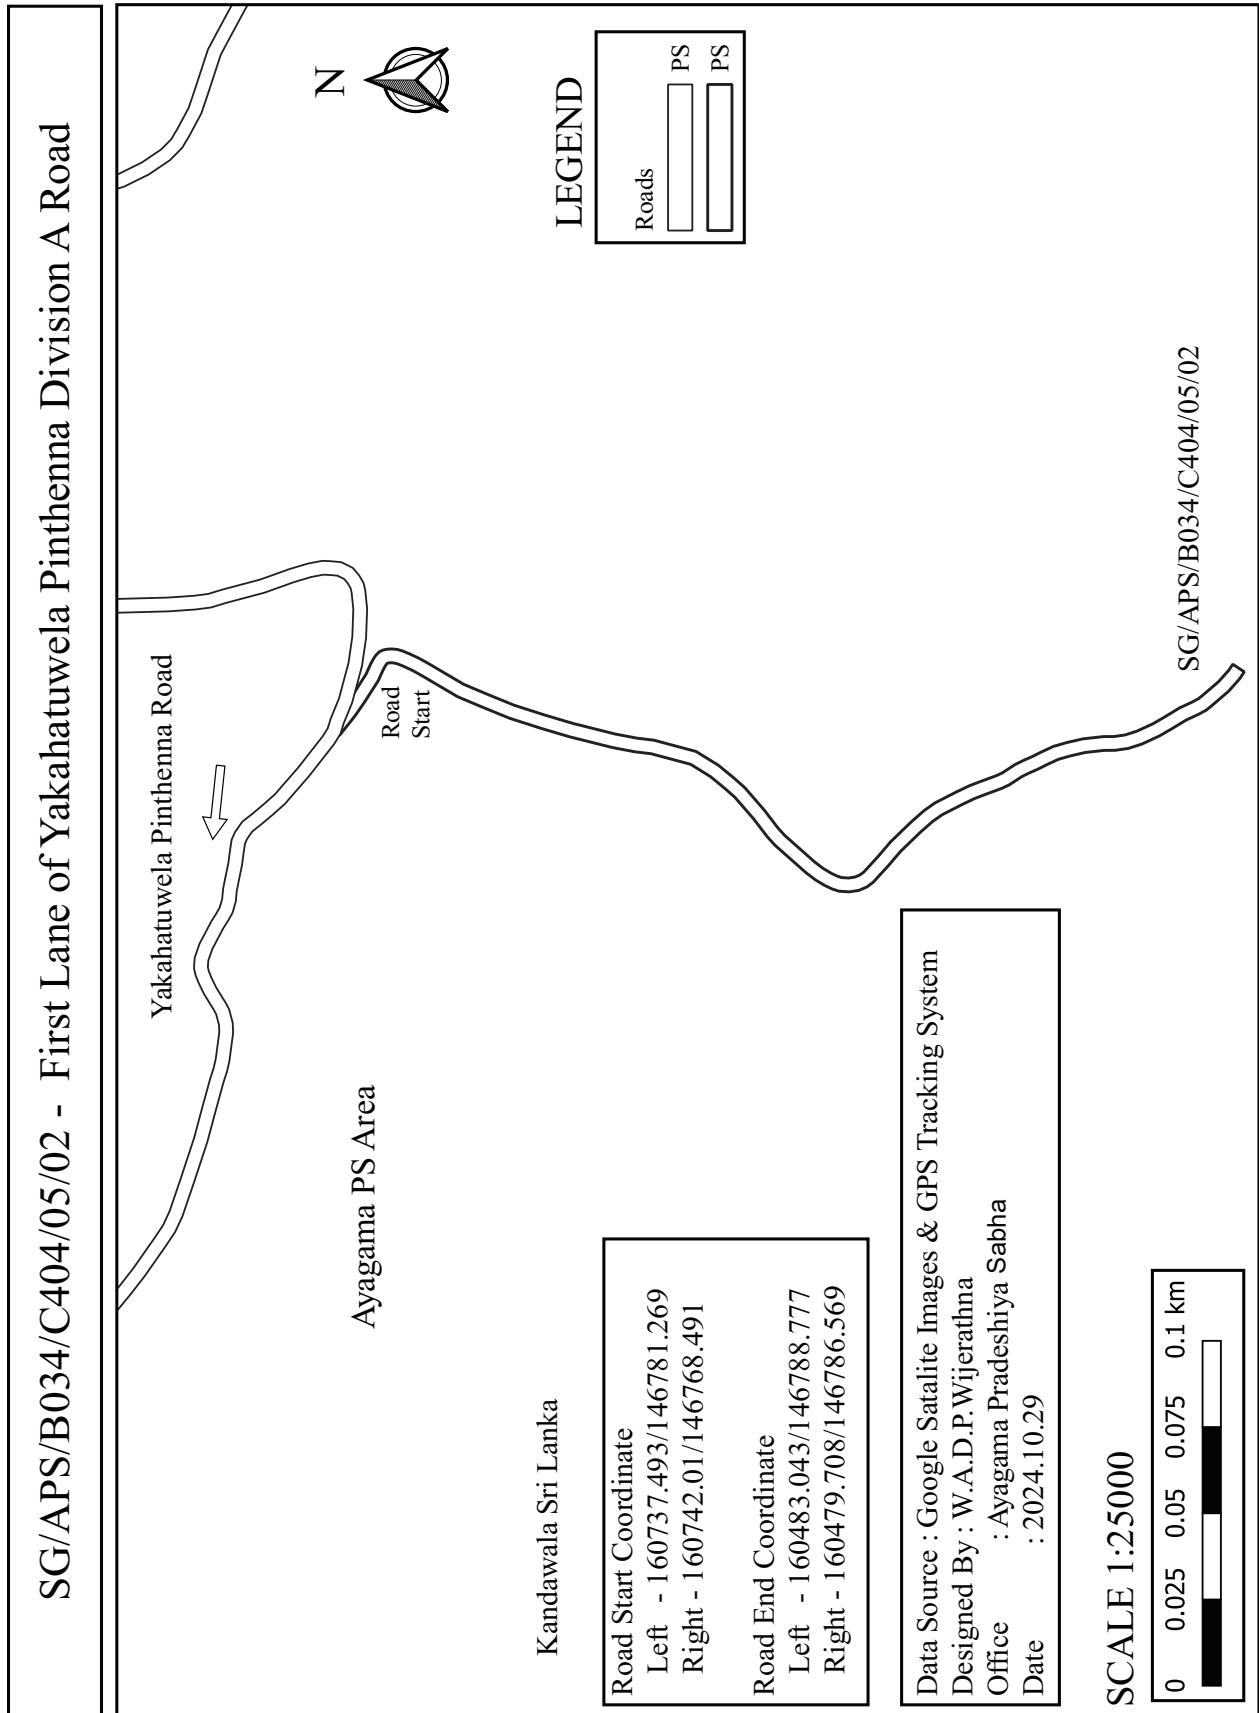


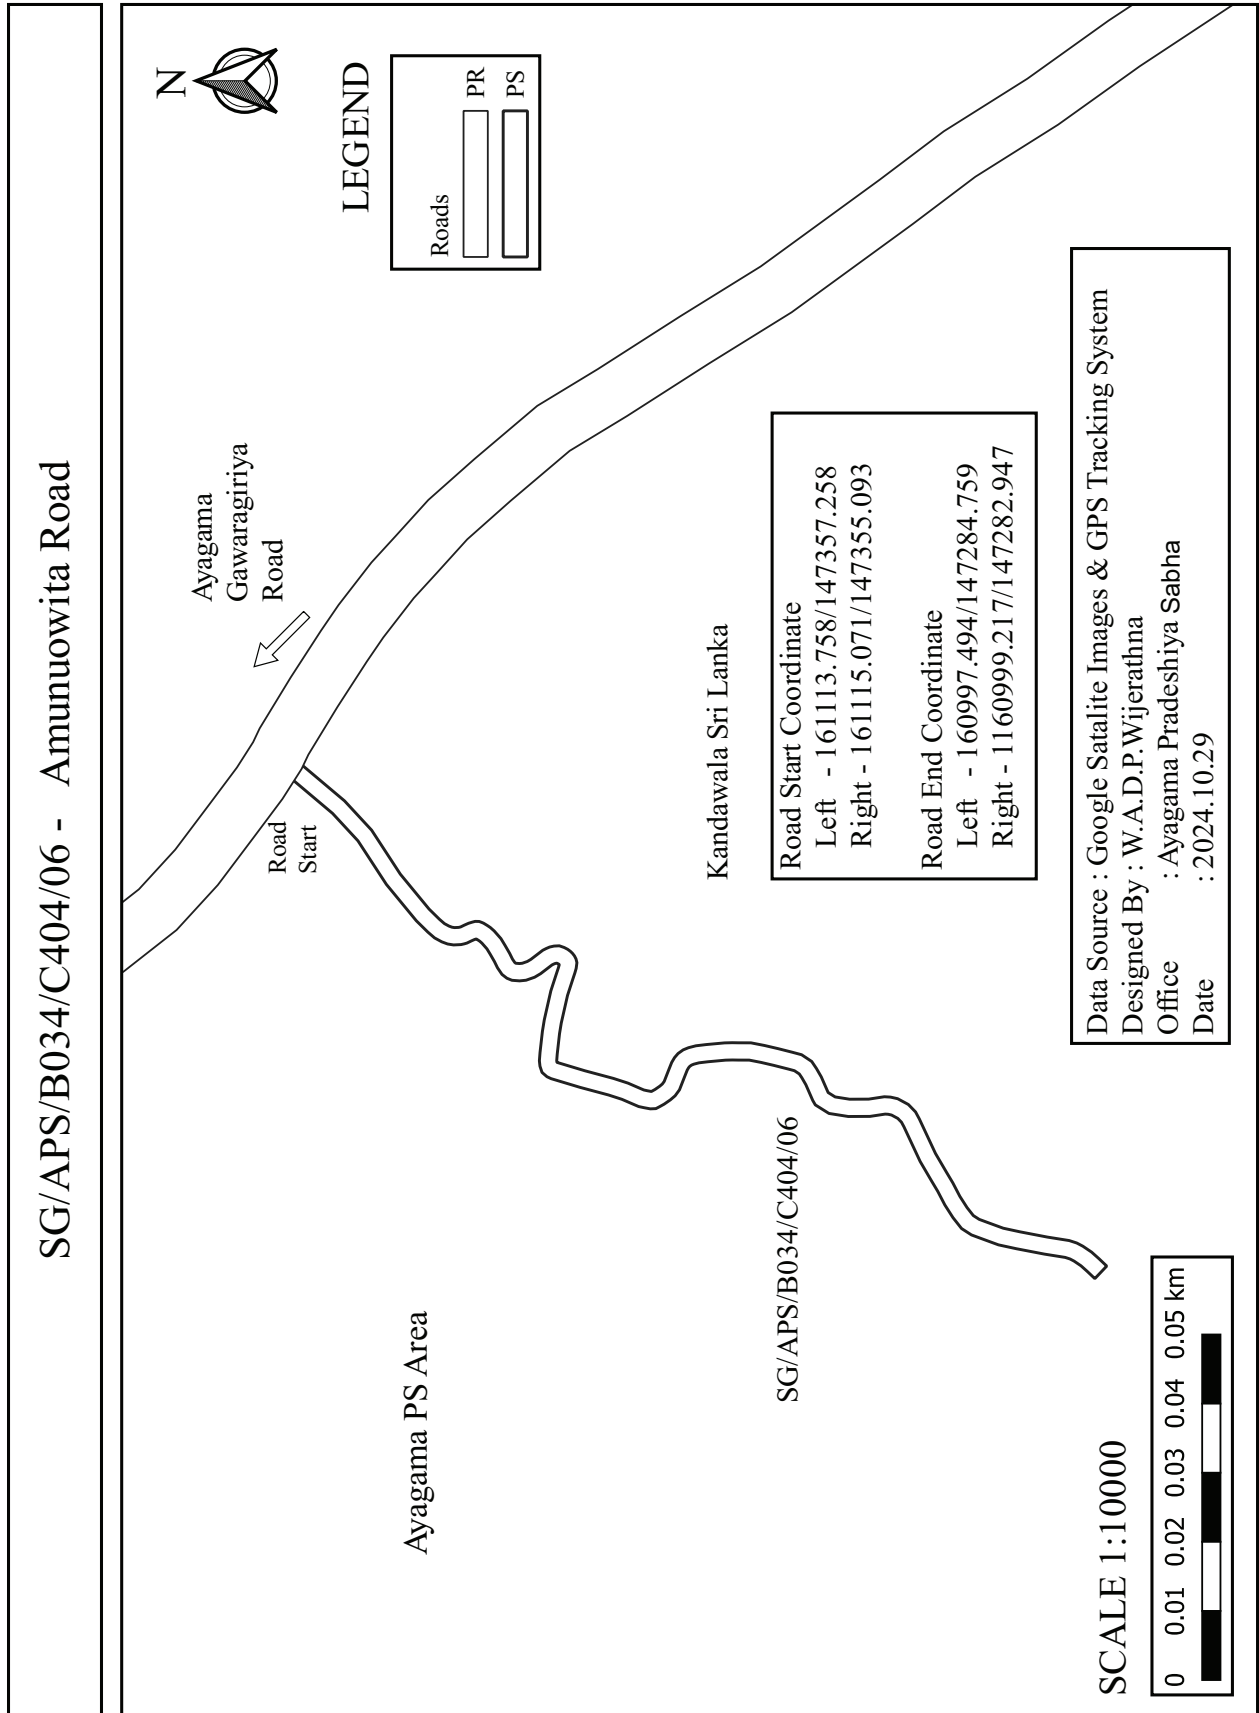

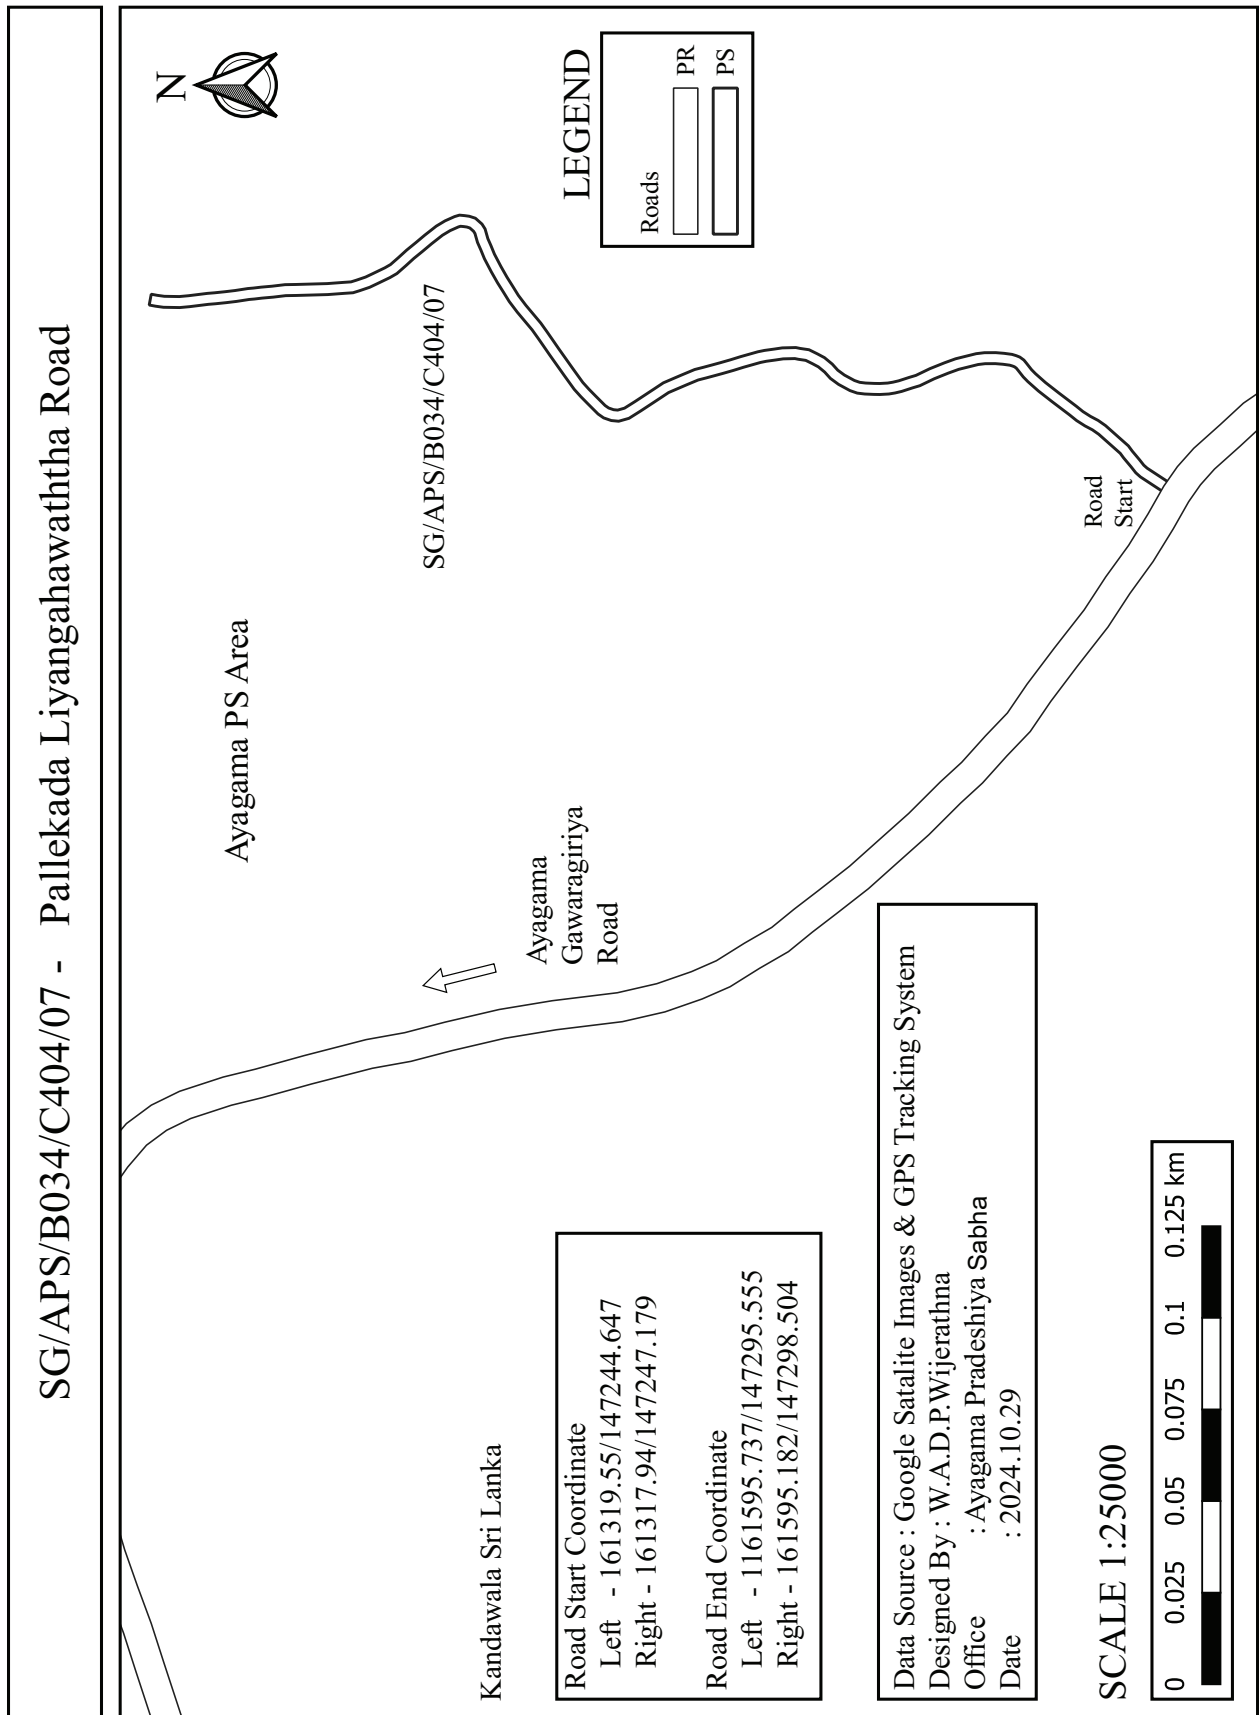



SG/APS/B034/C404/08 - Pallekada Kalatuwakanda Road

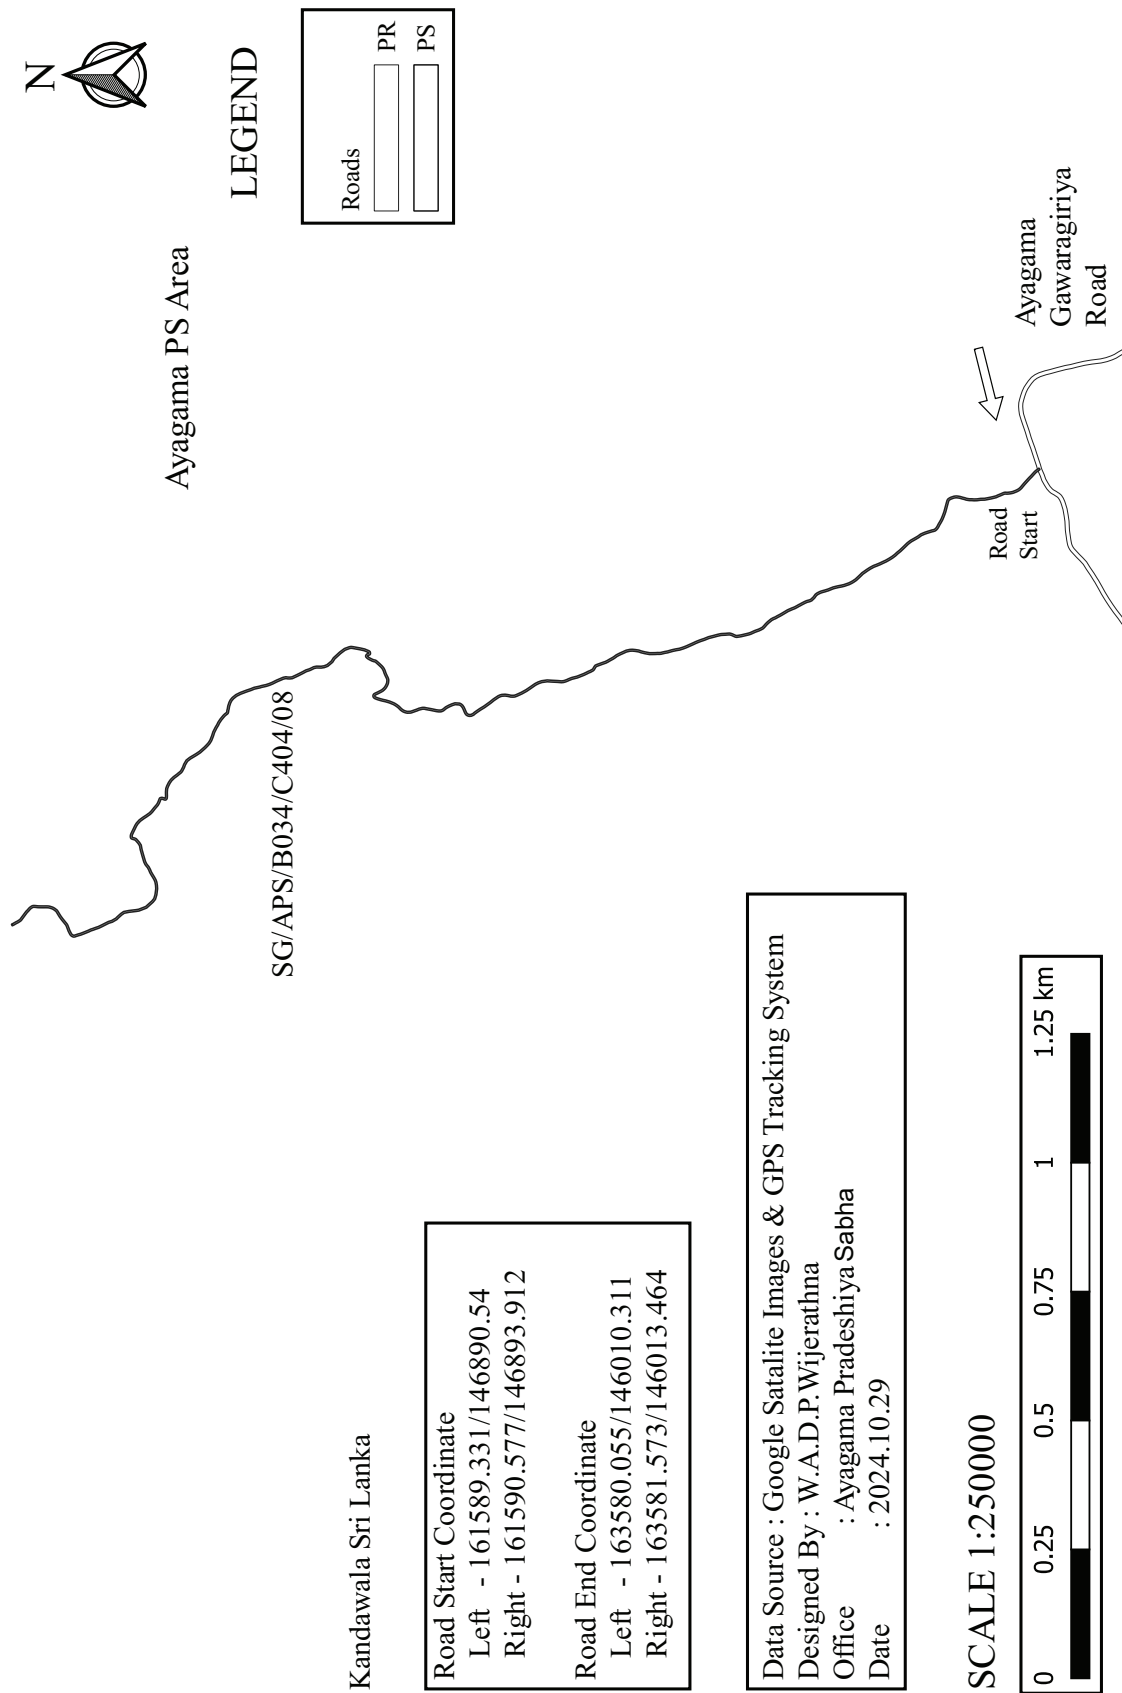


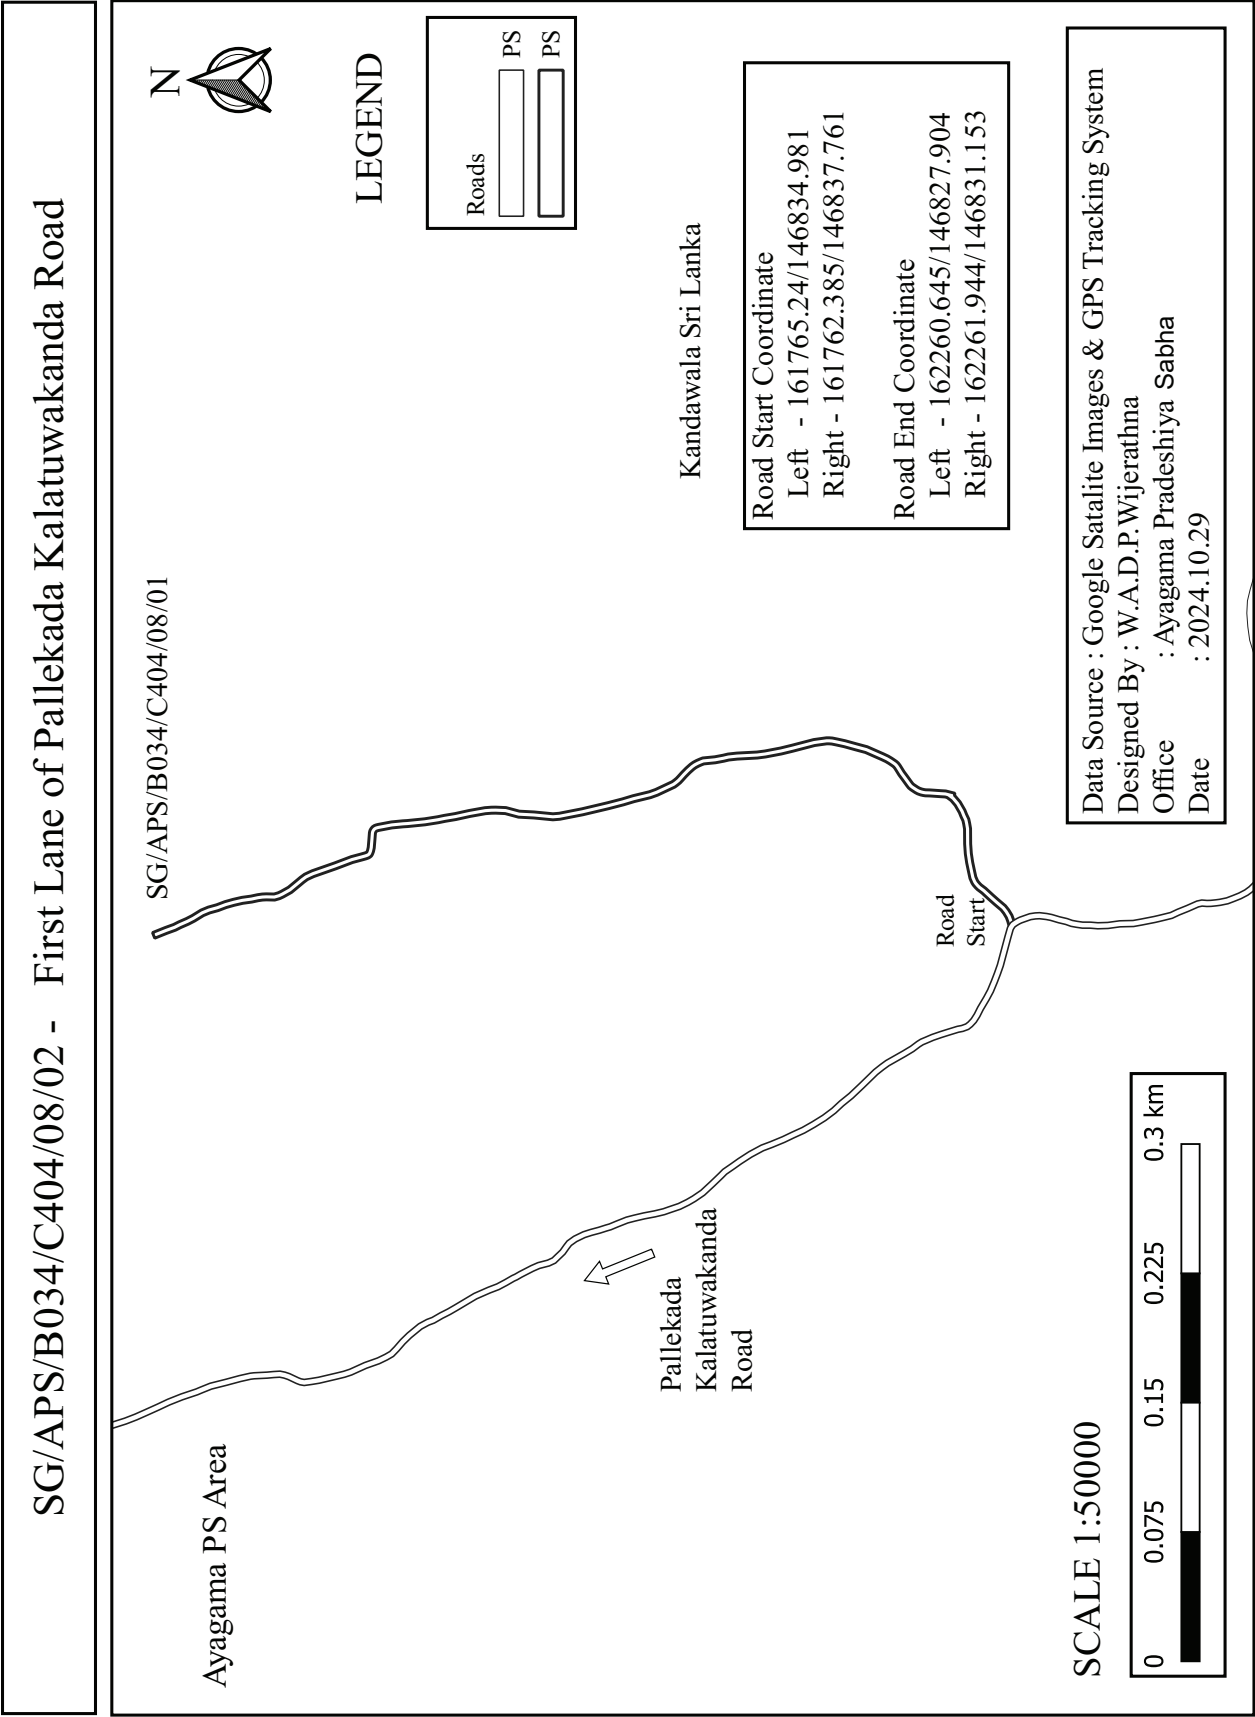



SG/APS/B034/C404/08/01/01 - First By Pass of Pallekada Kalatuwakanda Road

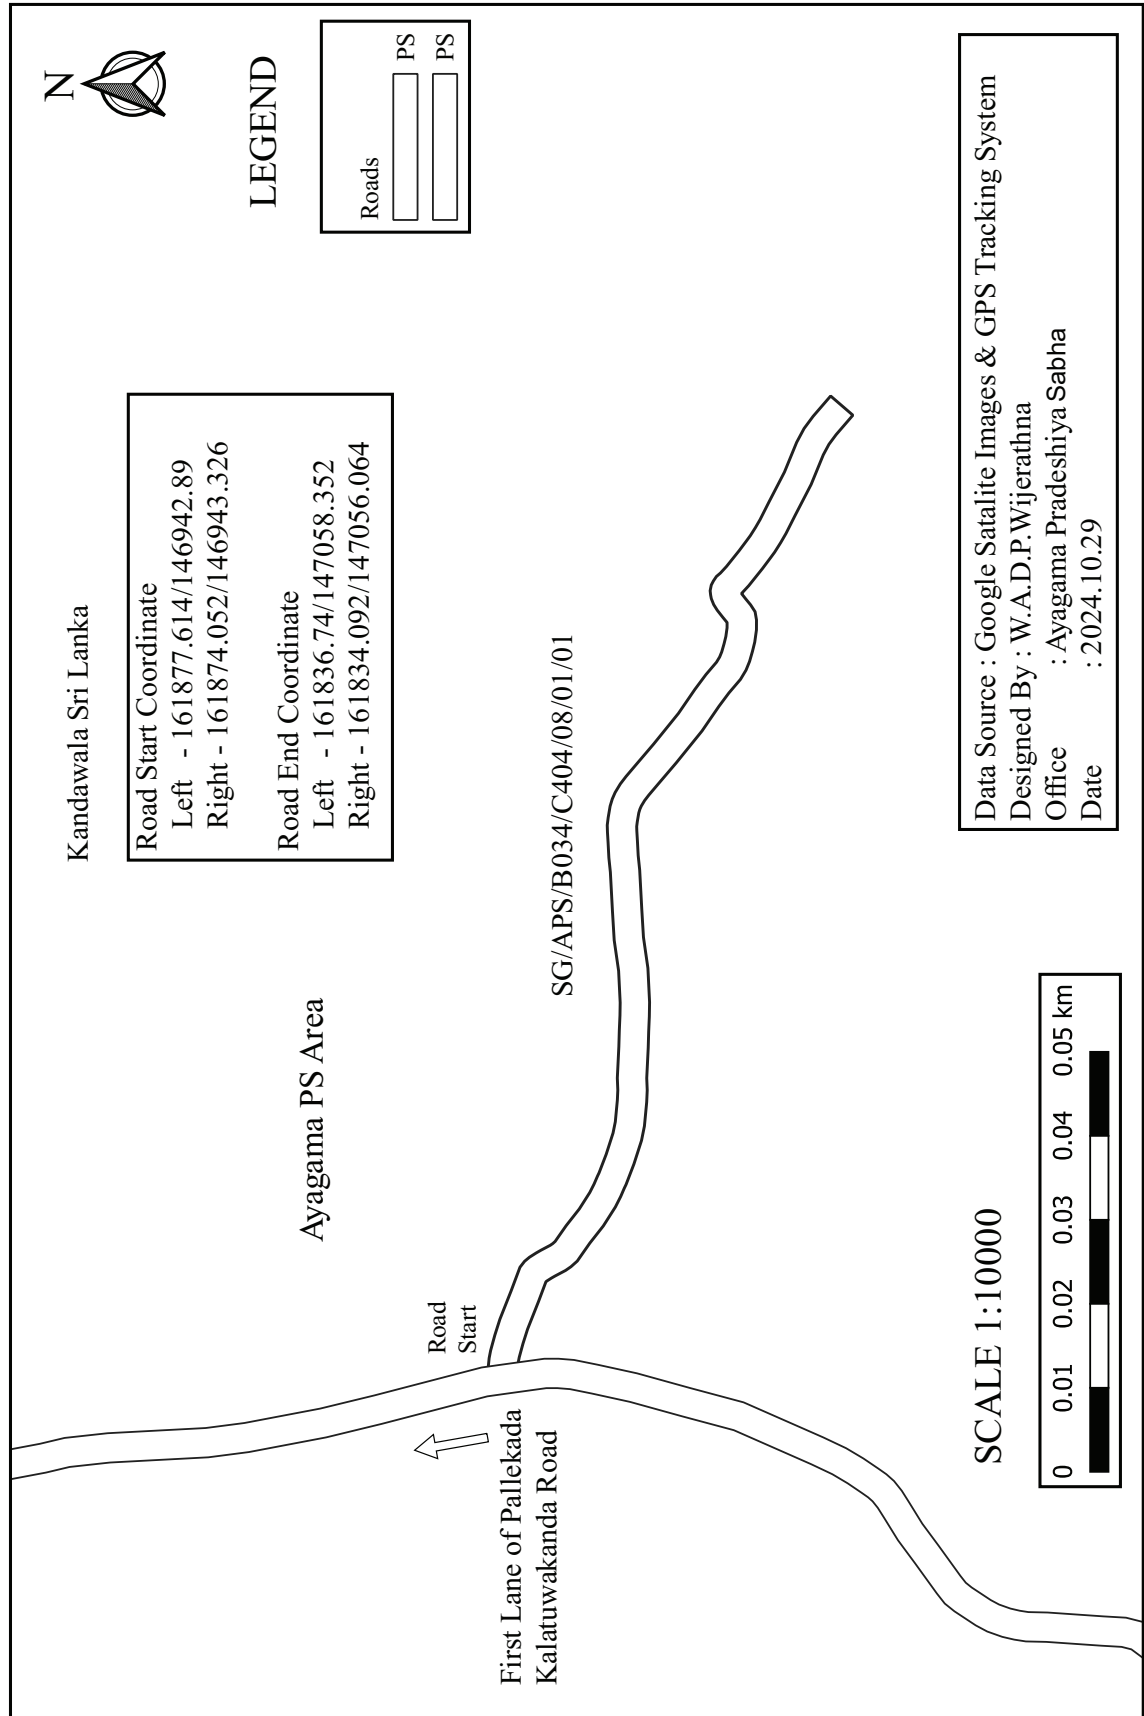


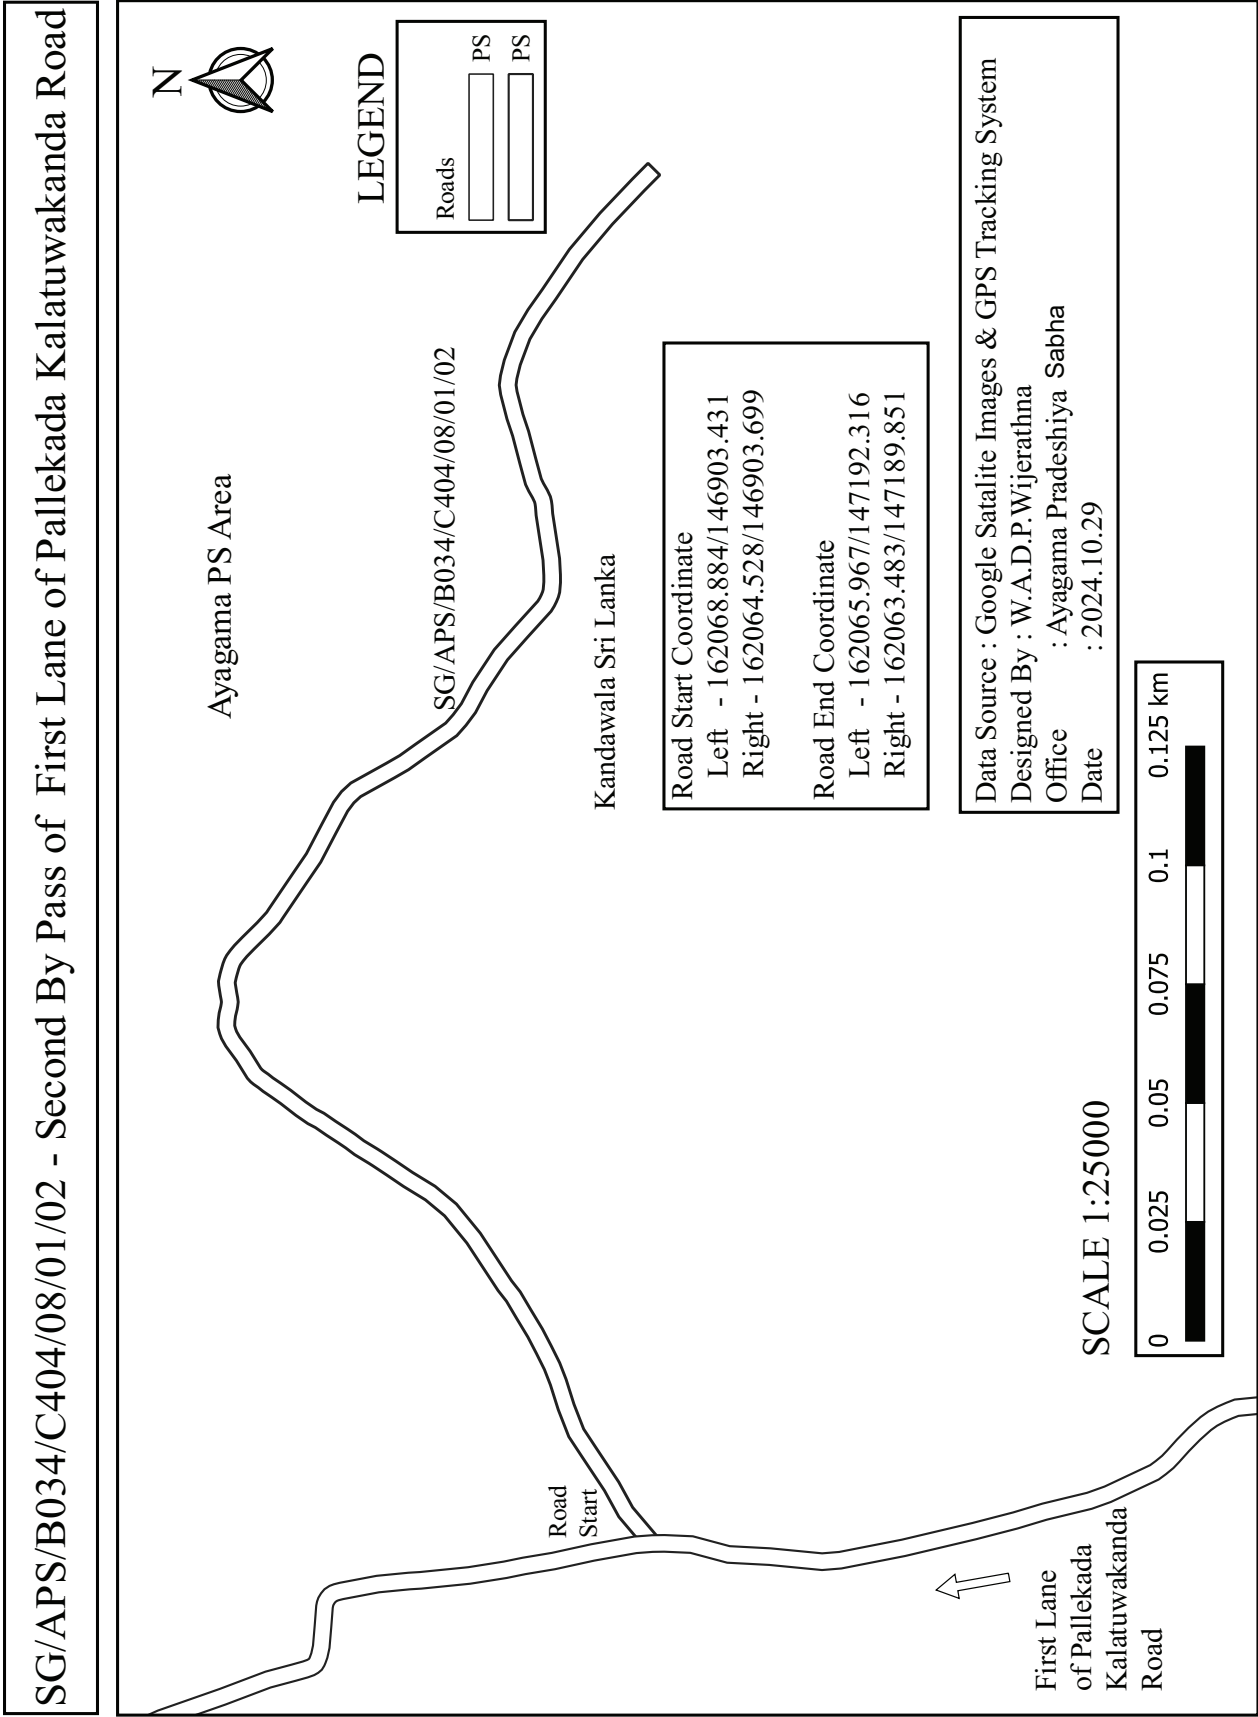


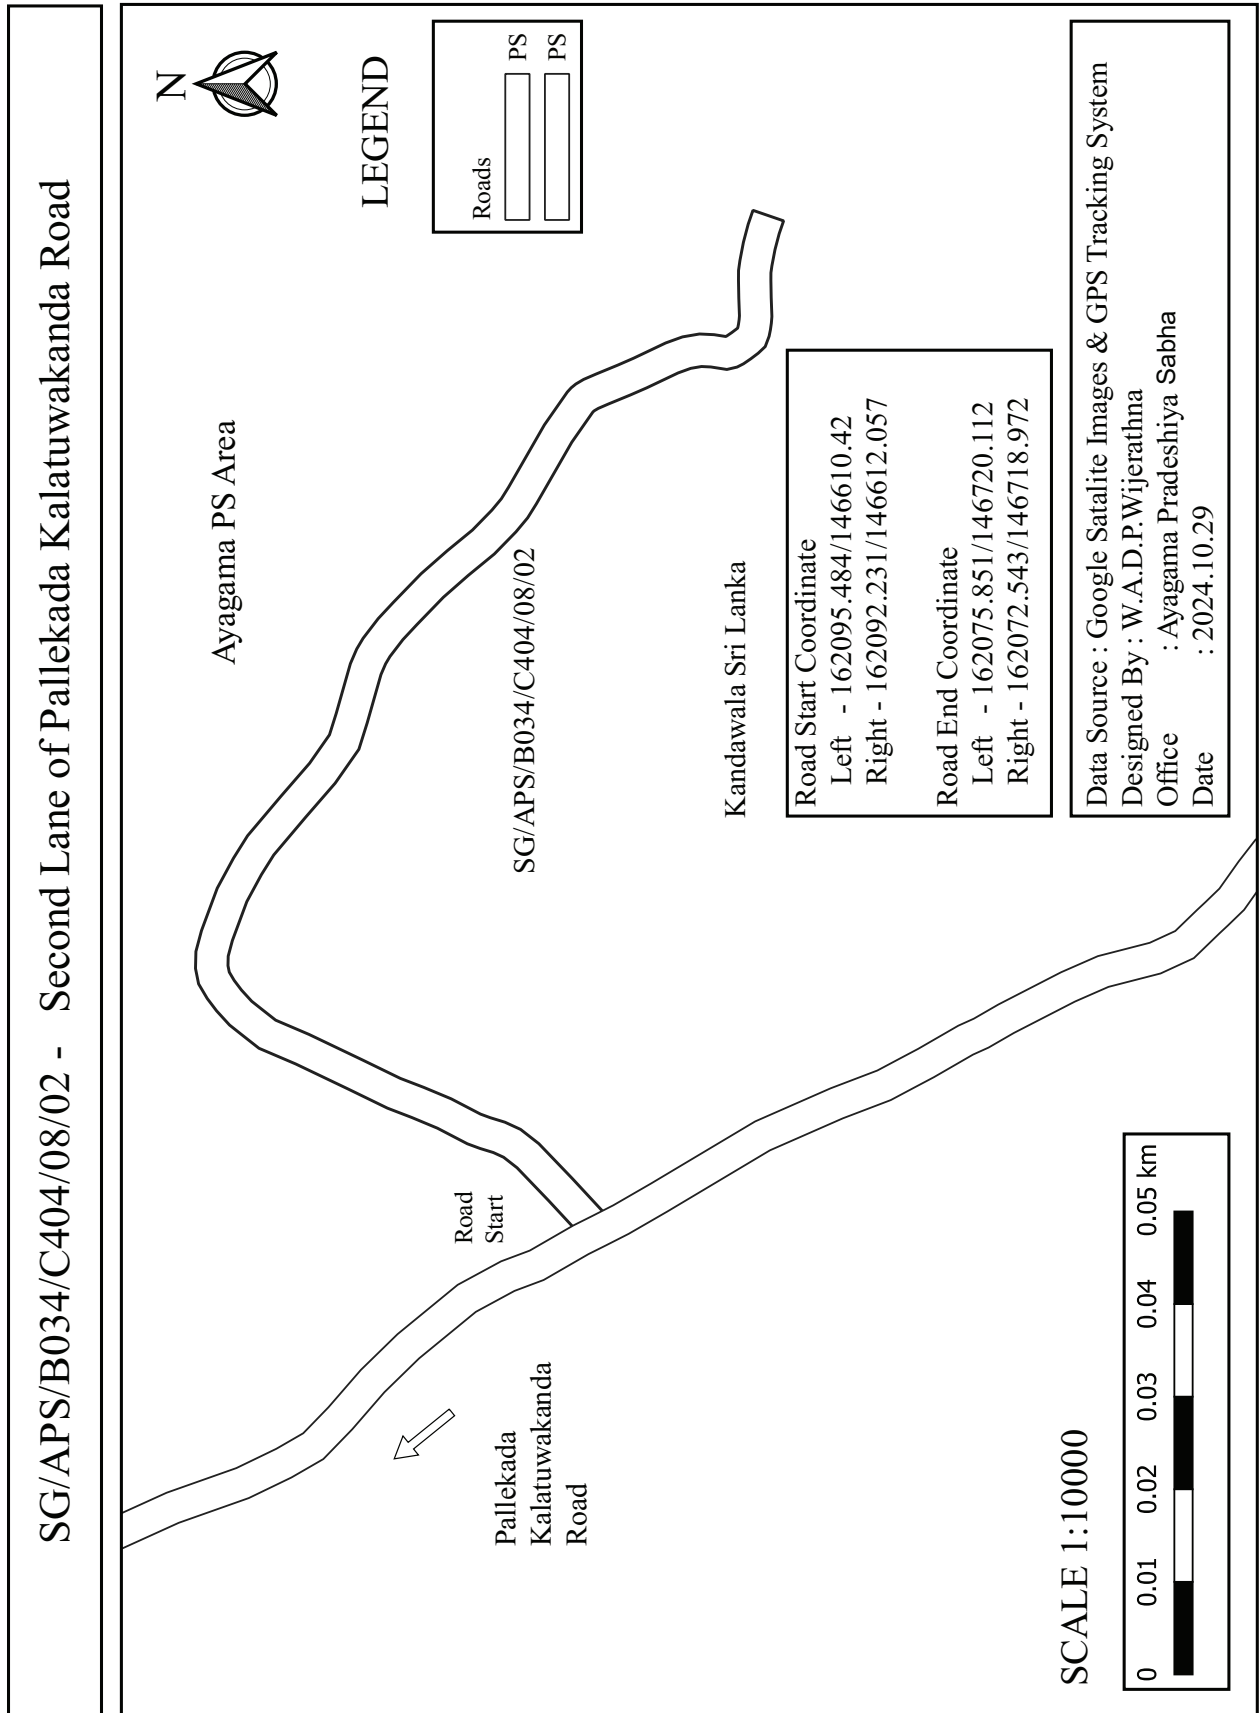


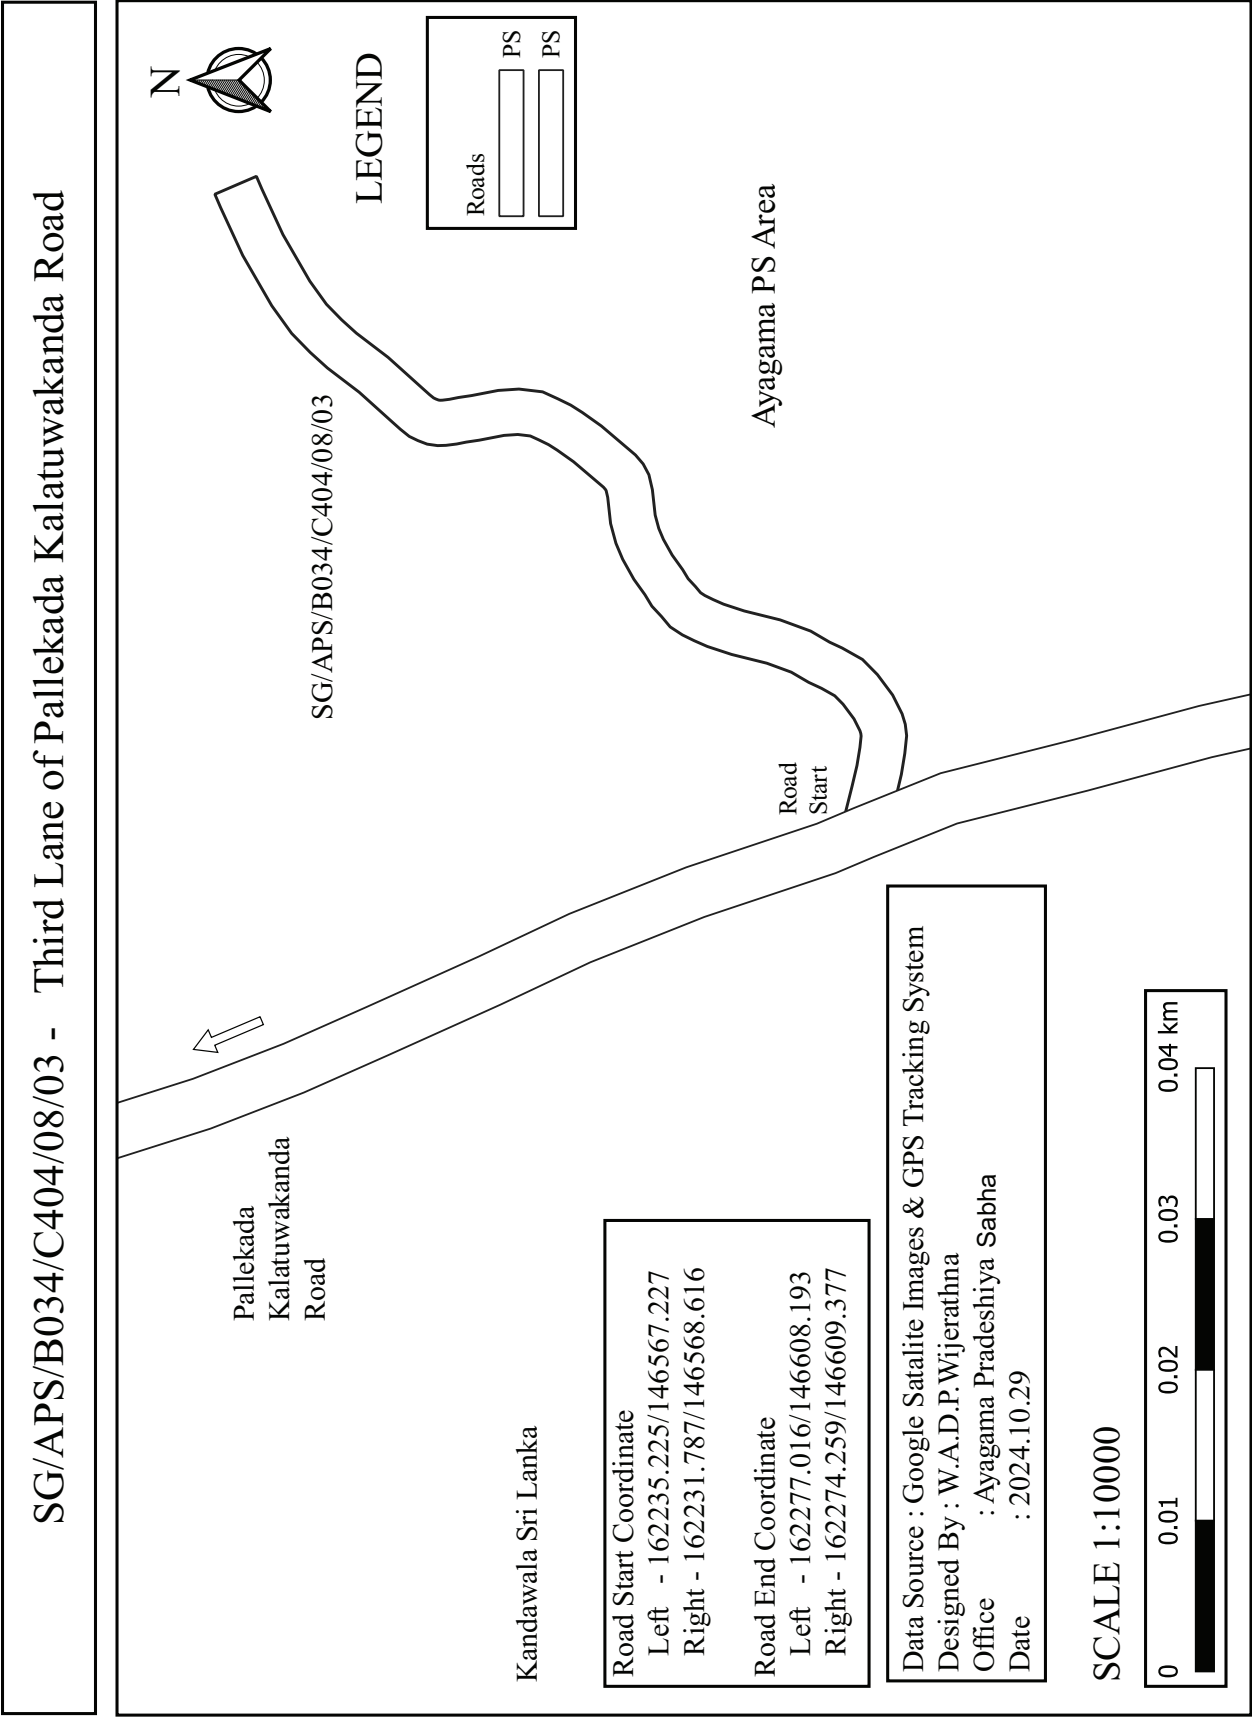

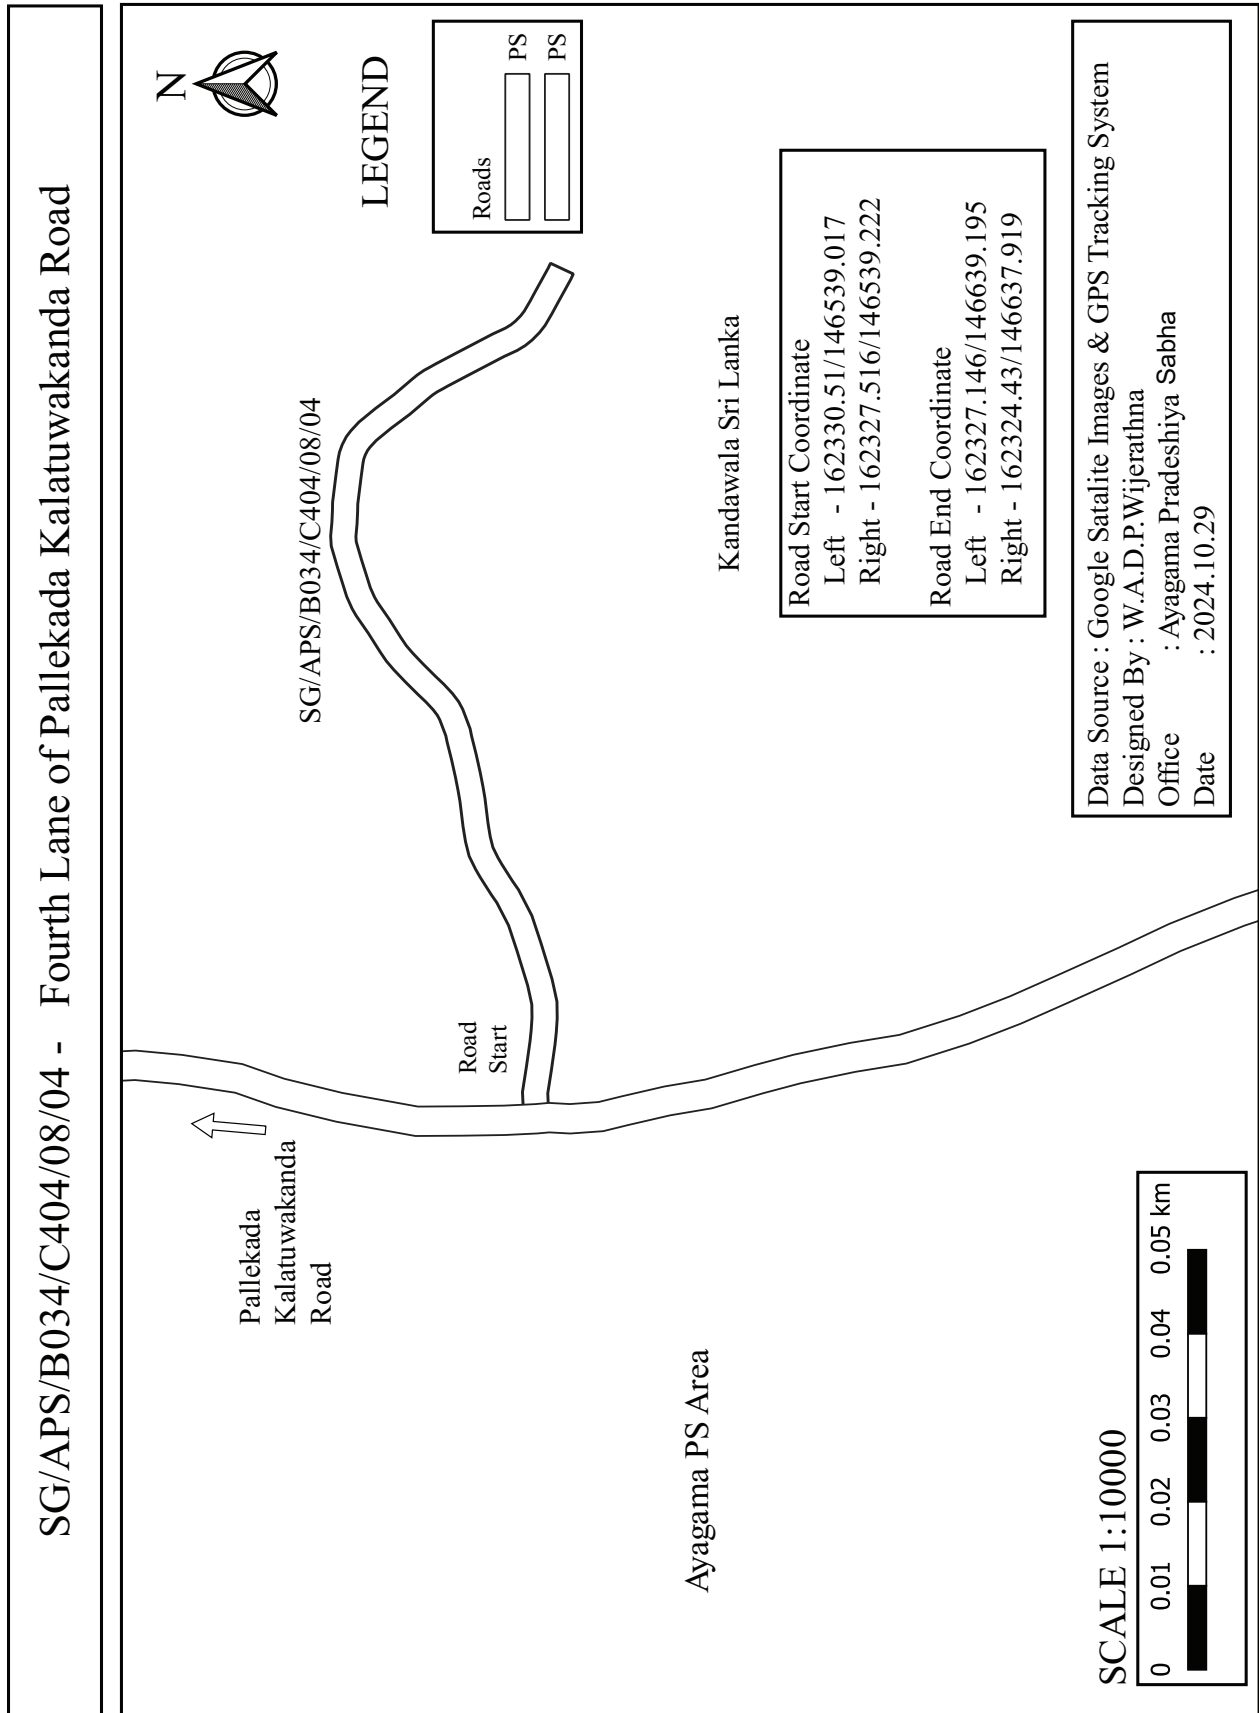


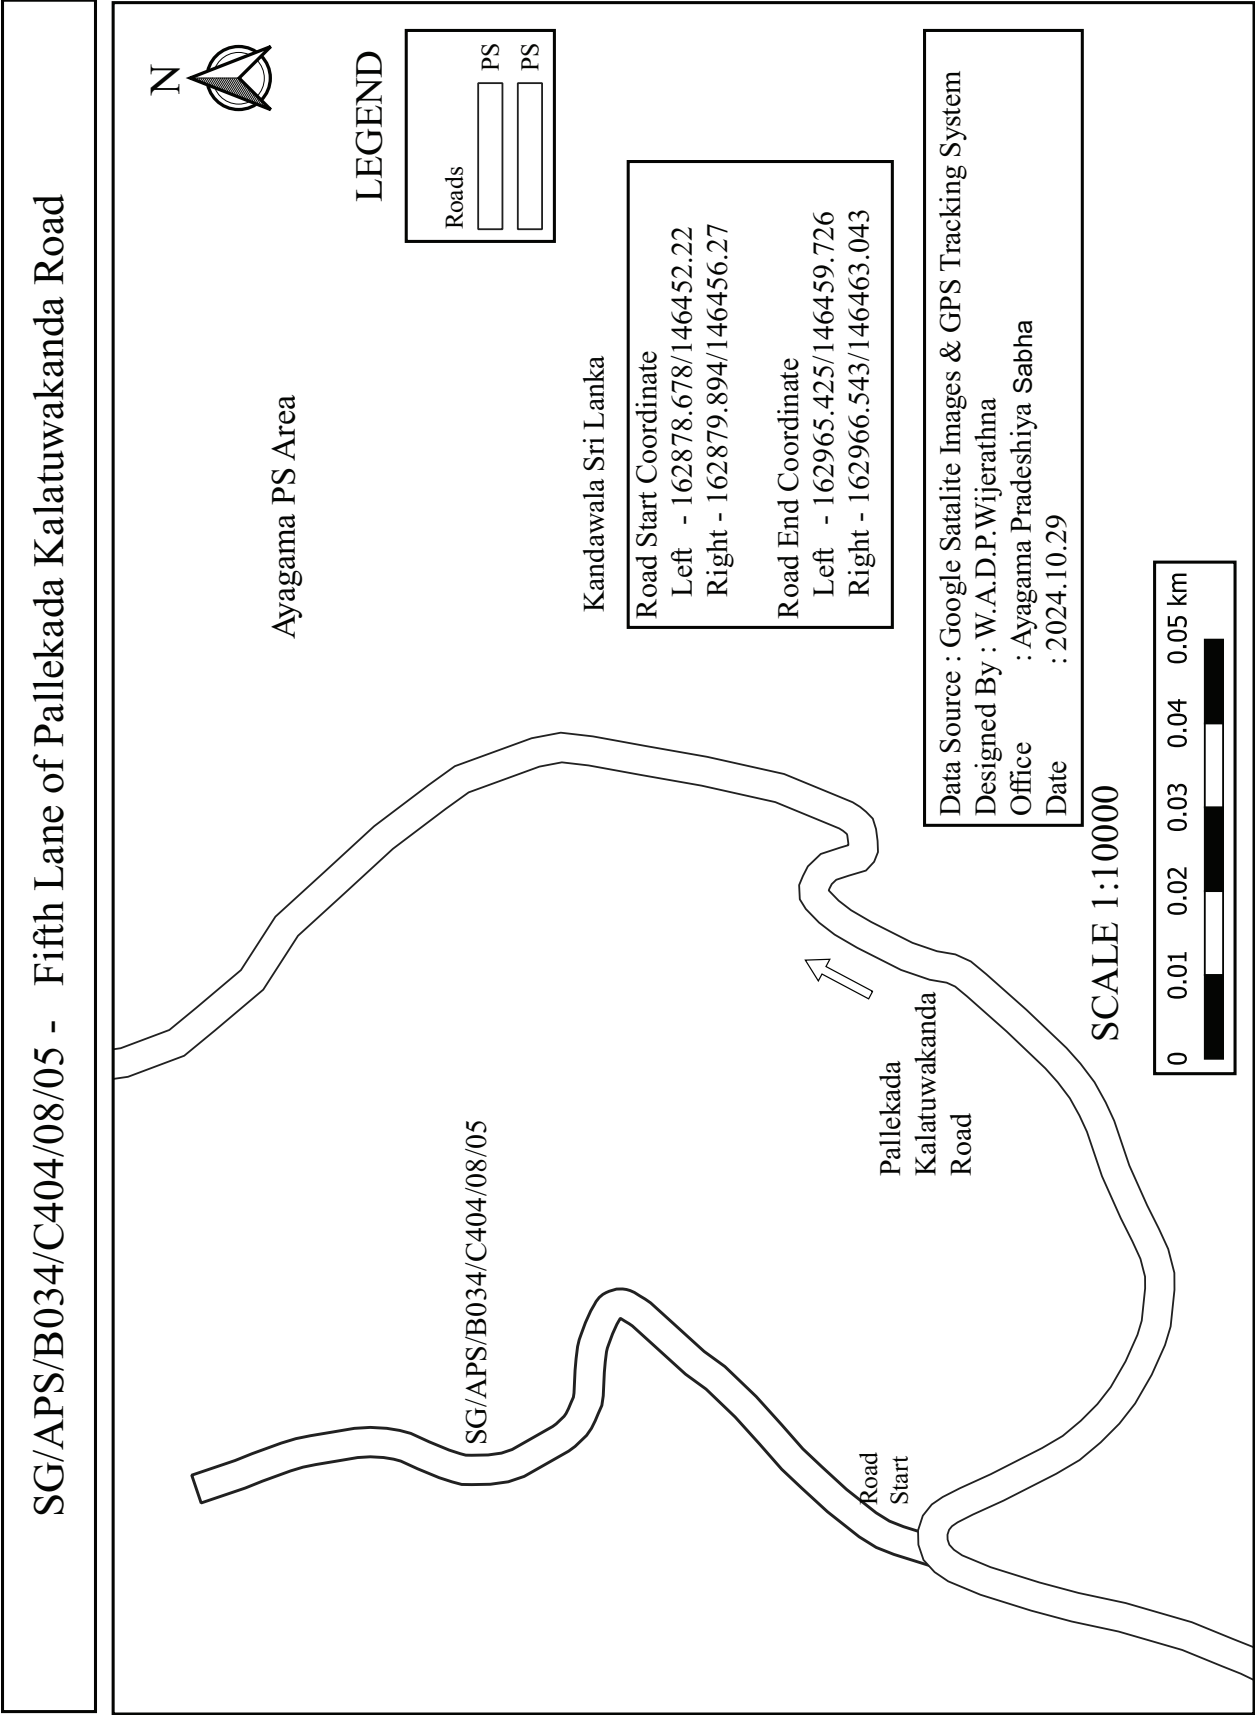


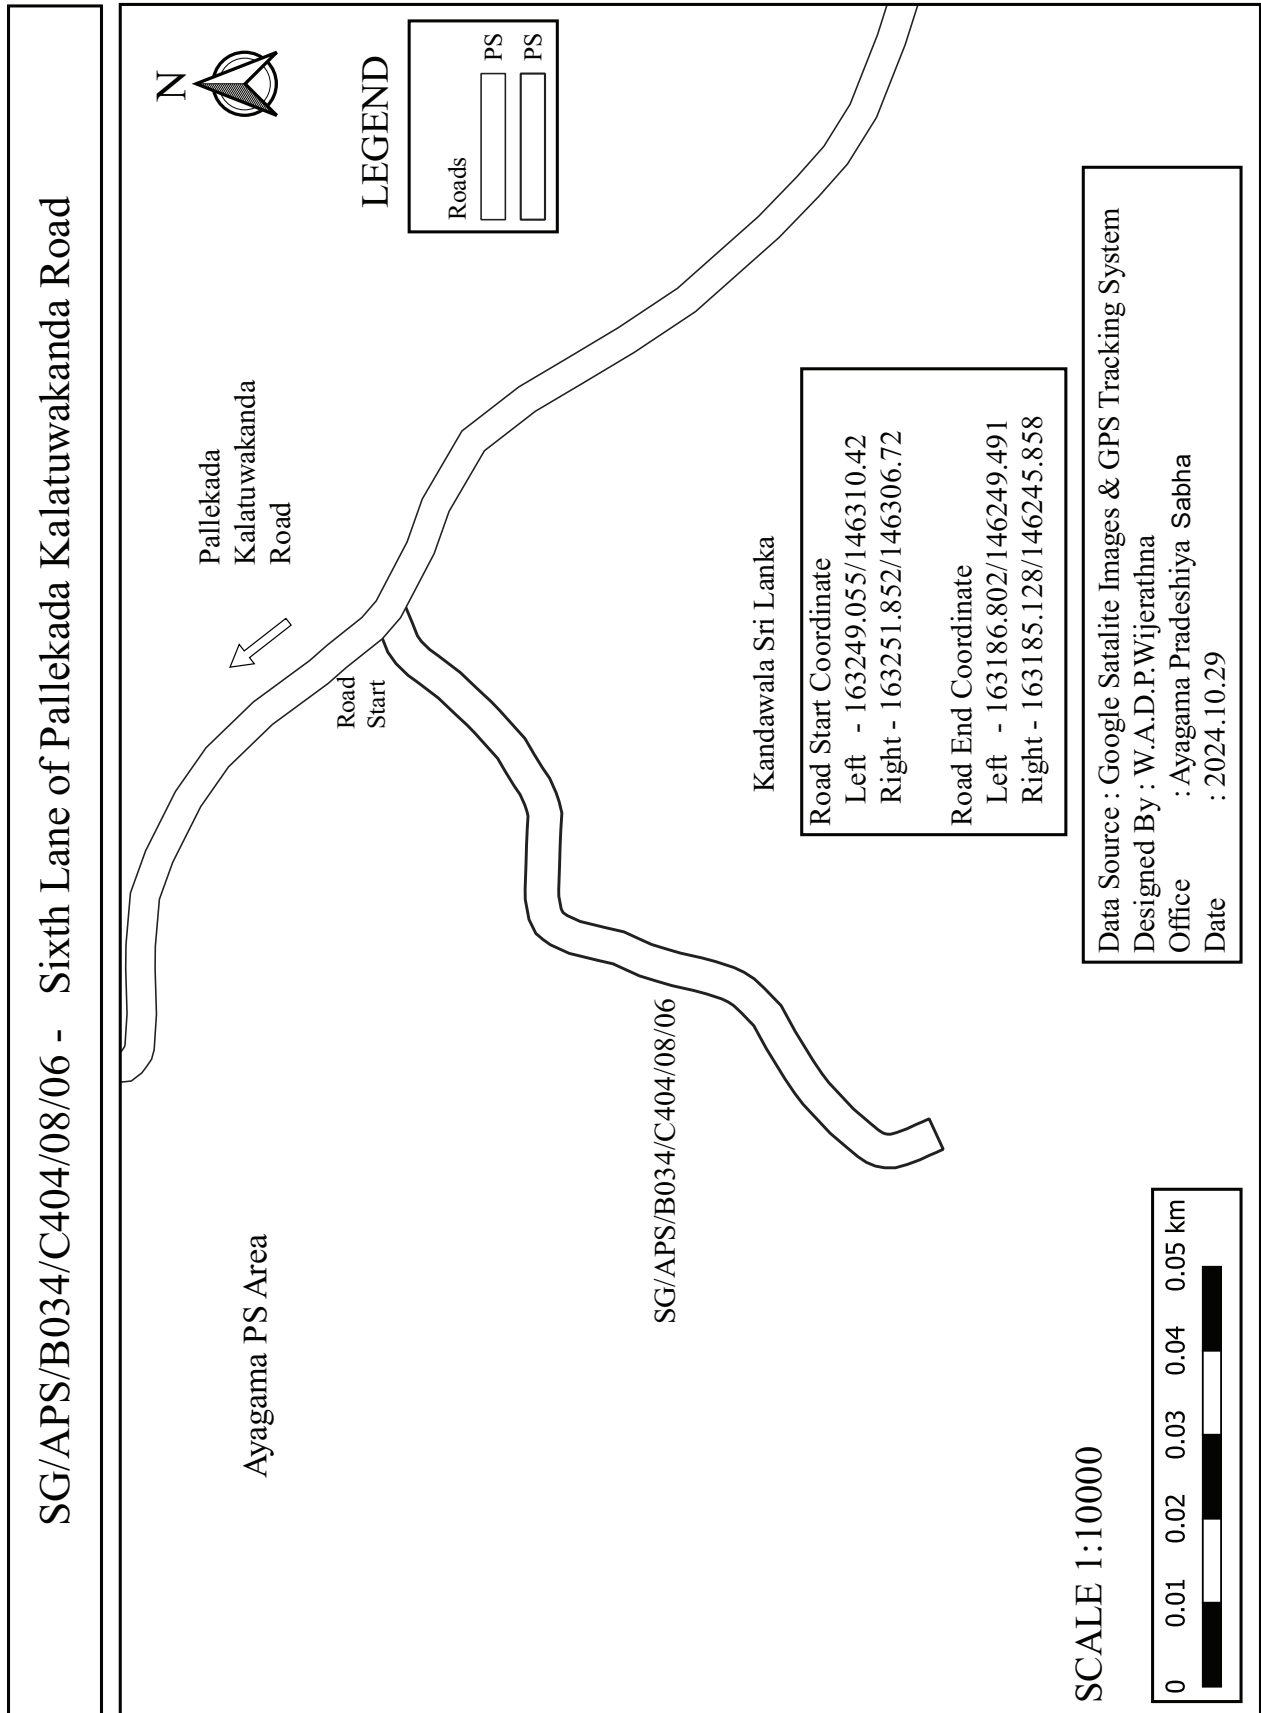

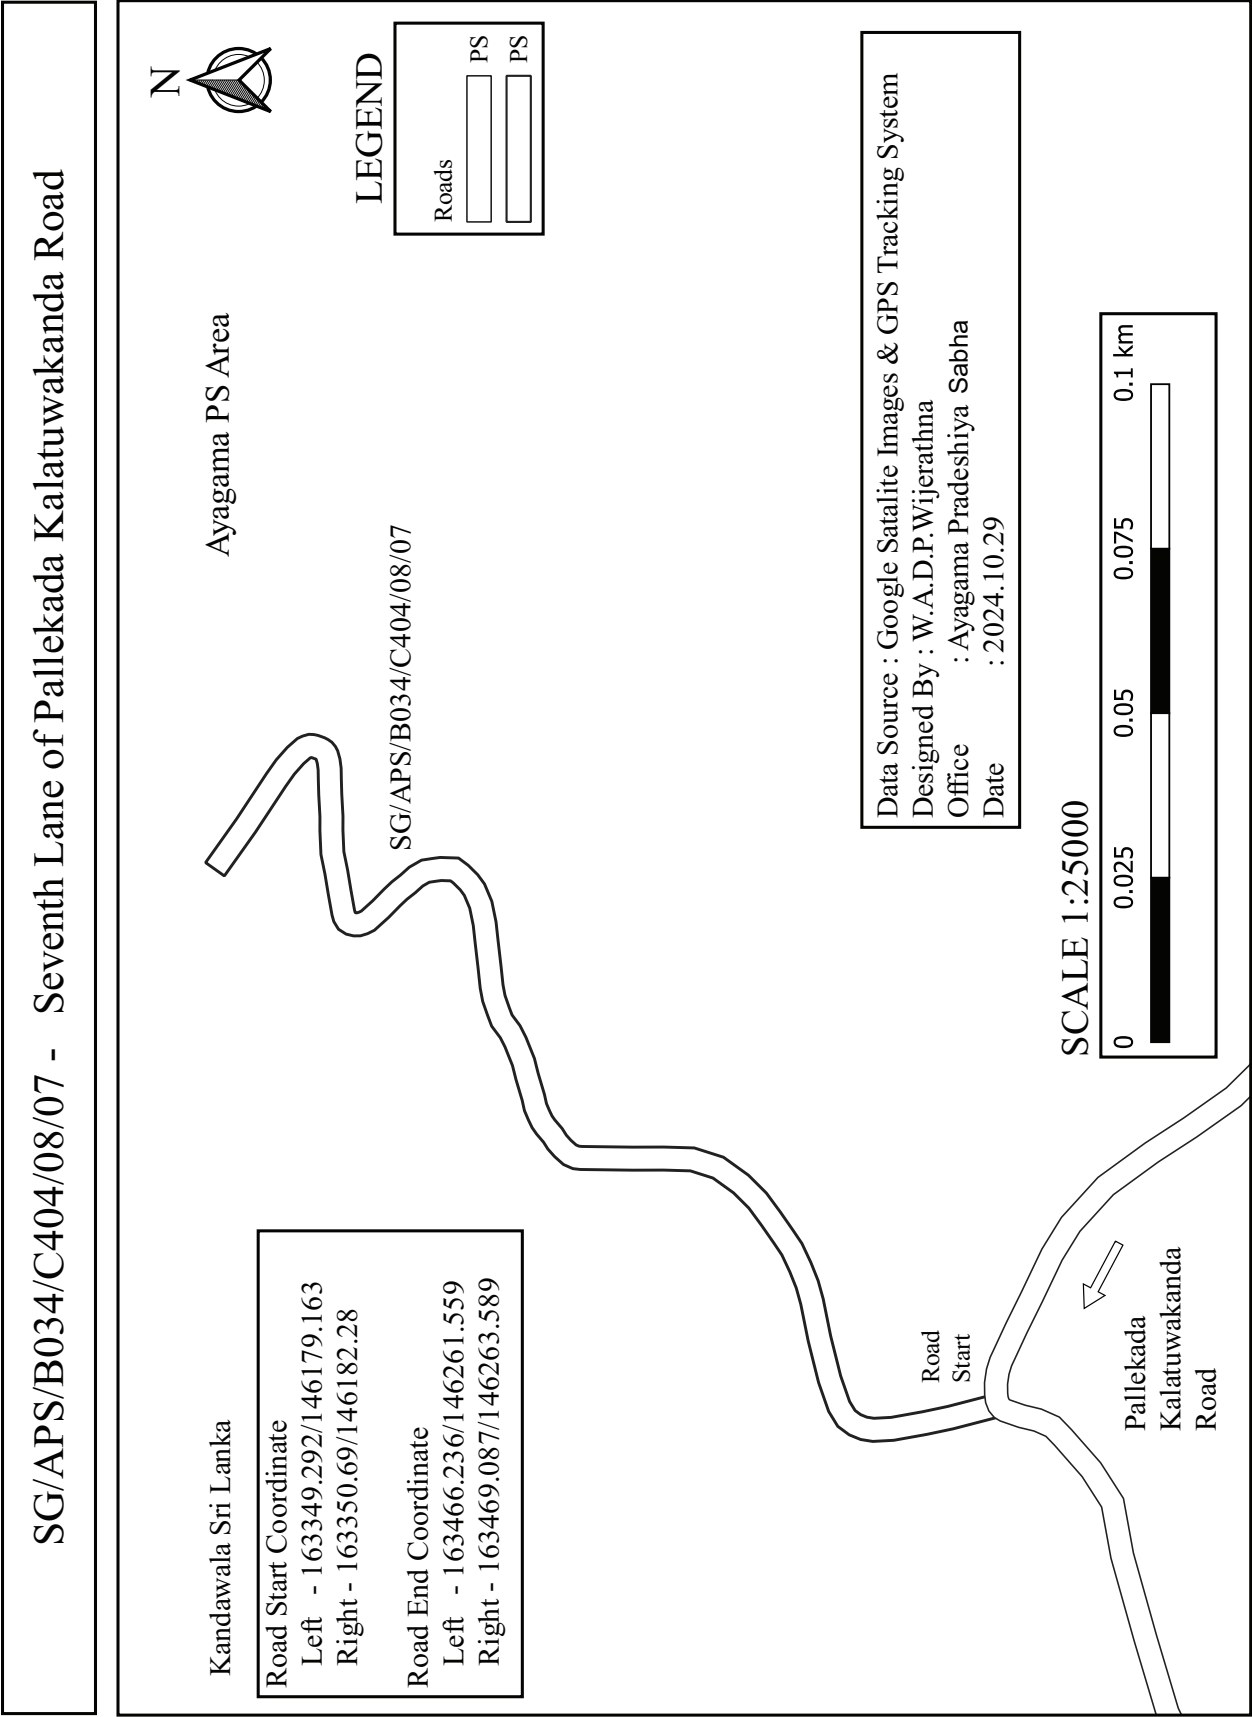


SG/APS/B034/C404/09 - Pallekada Witowita Road

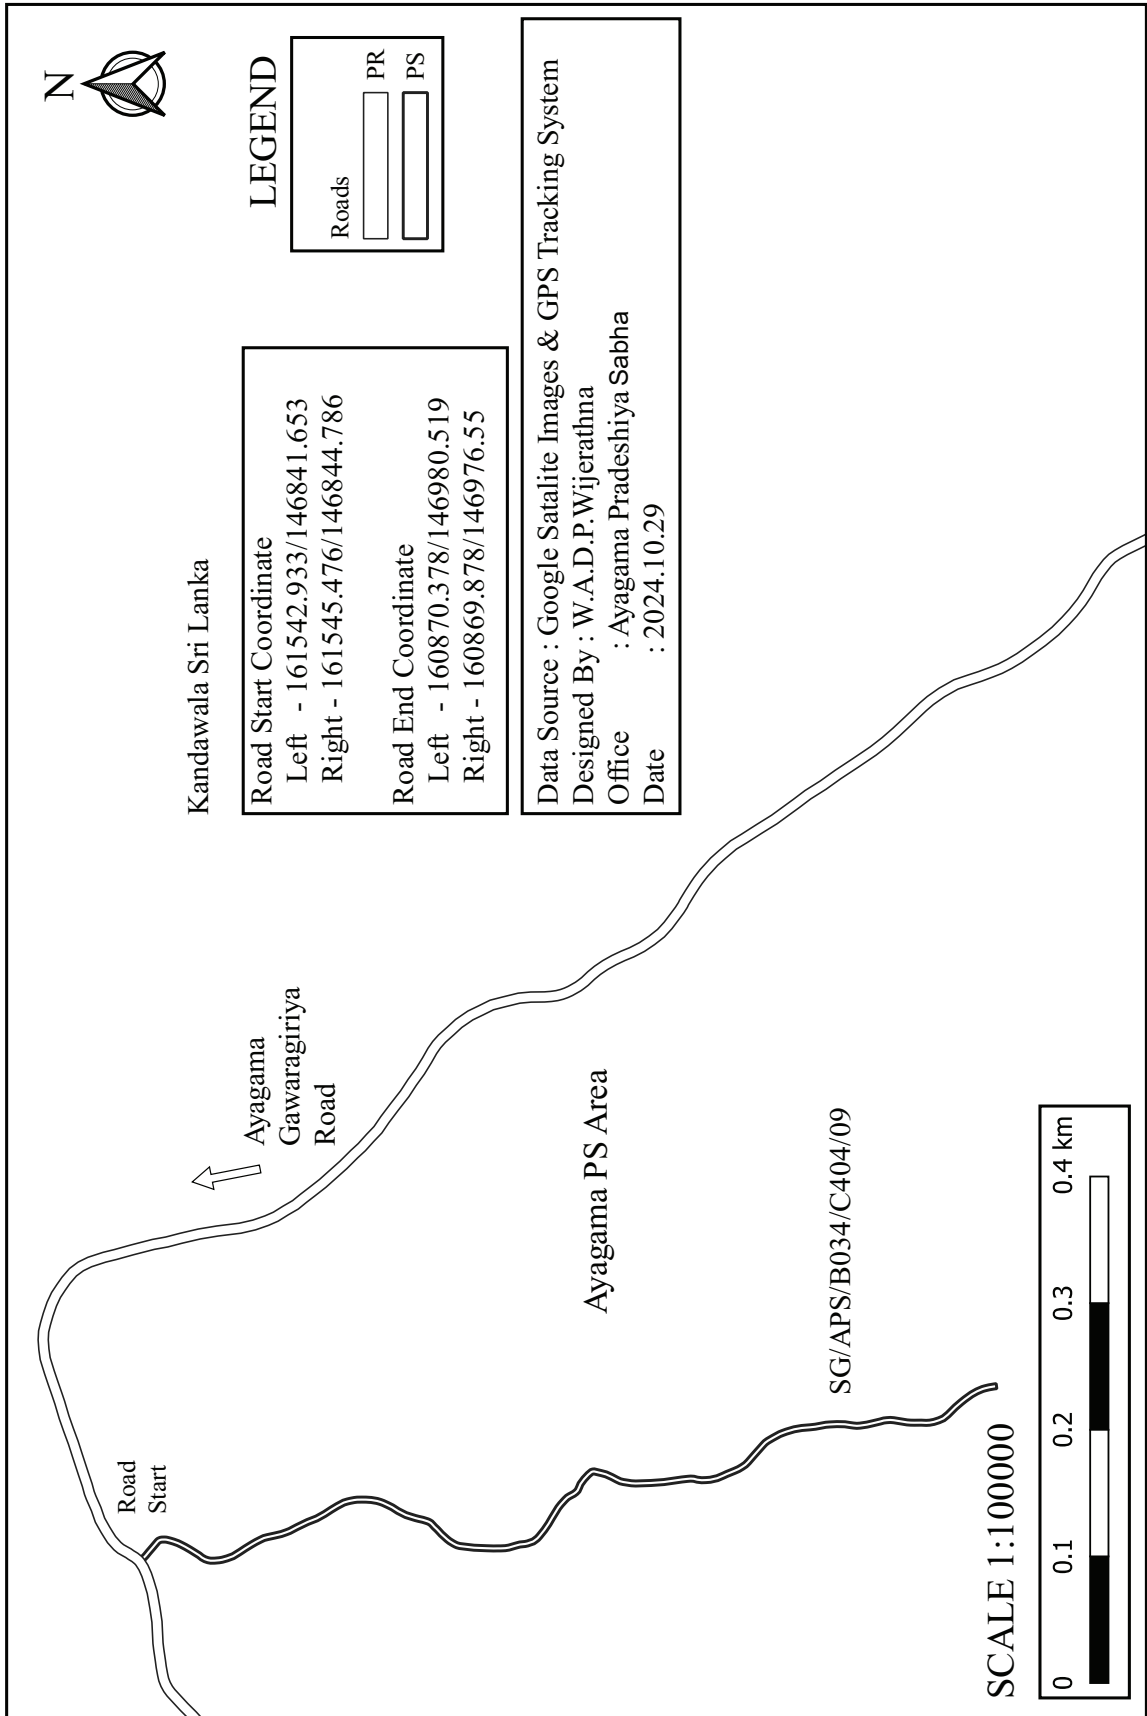


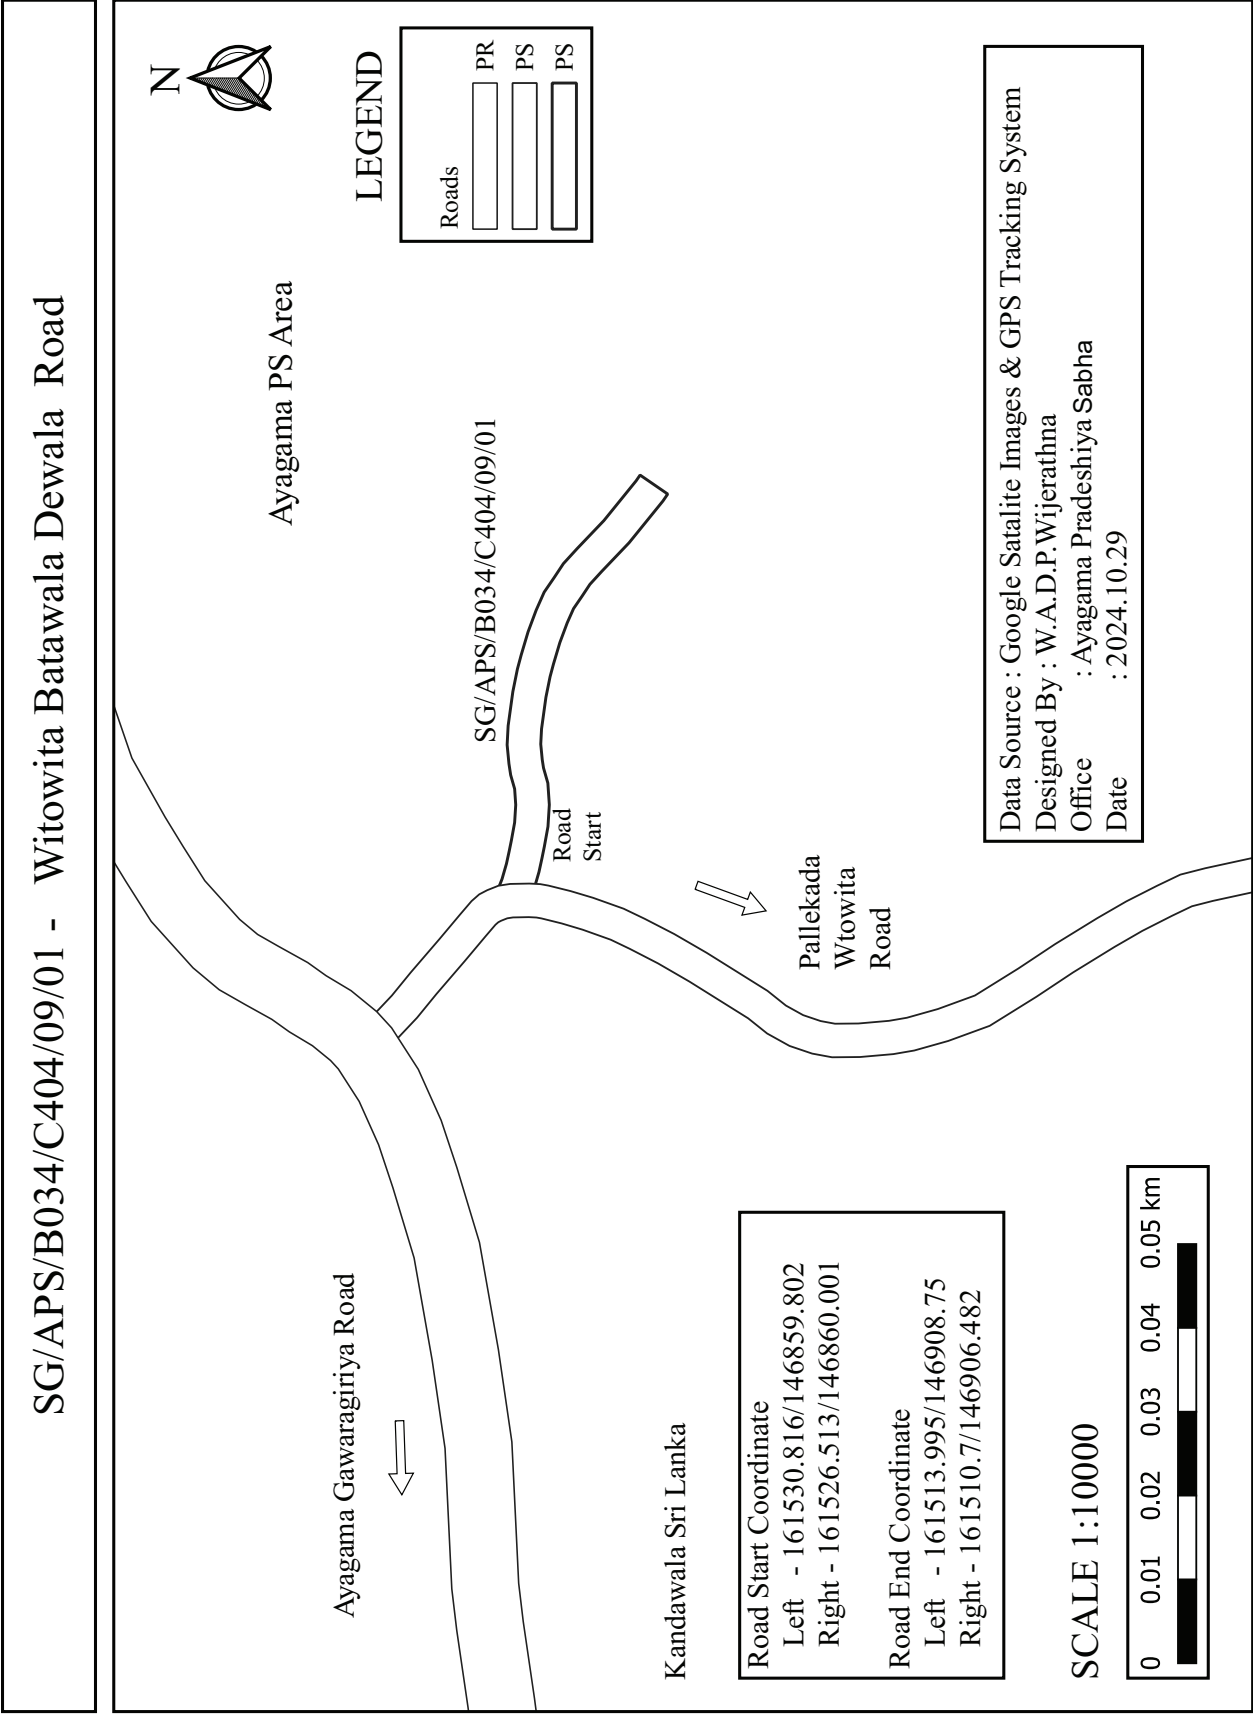



SG/APS/B034/C404/09/02 - First Lane of Pallekada Witowita Road

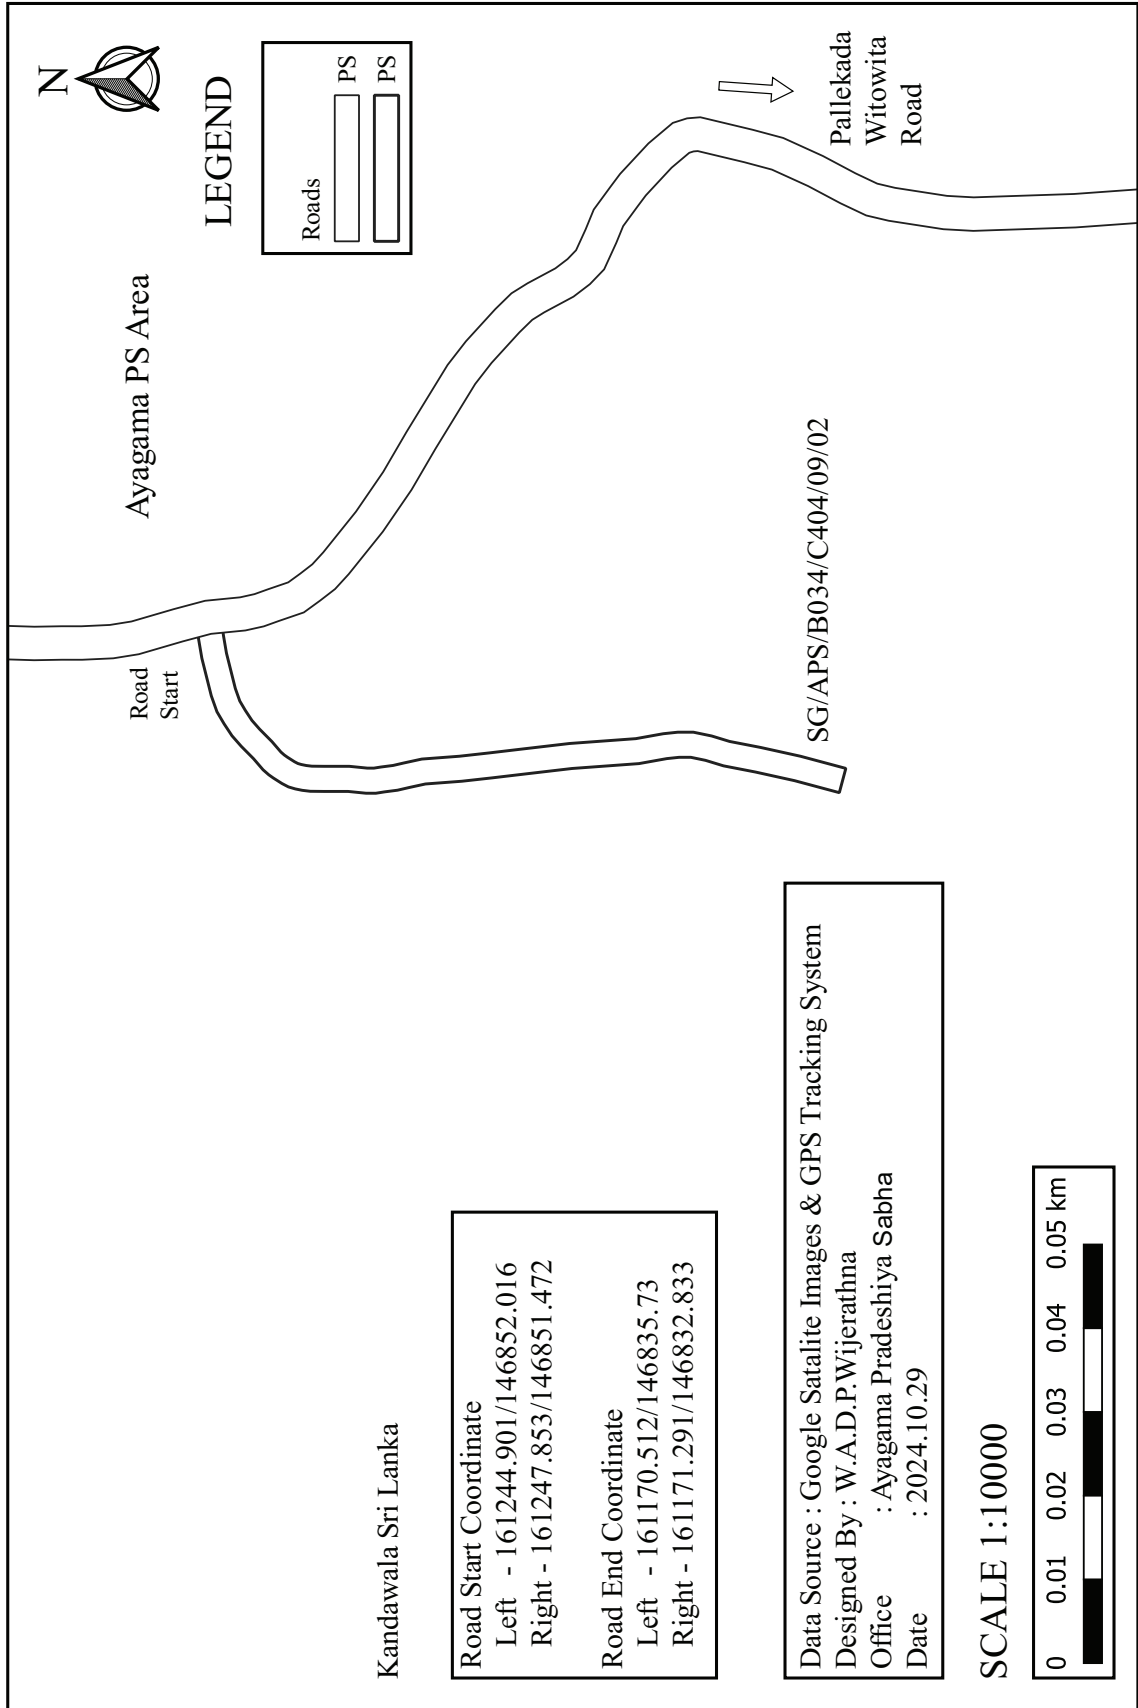



Kandawala Sri Lanka

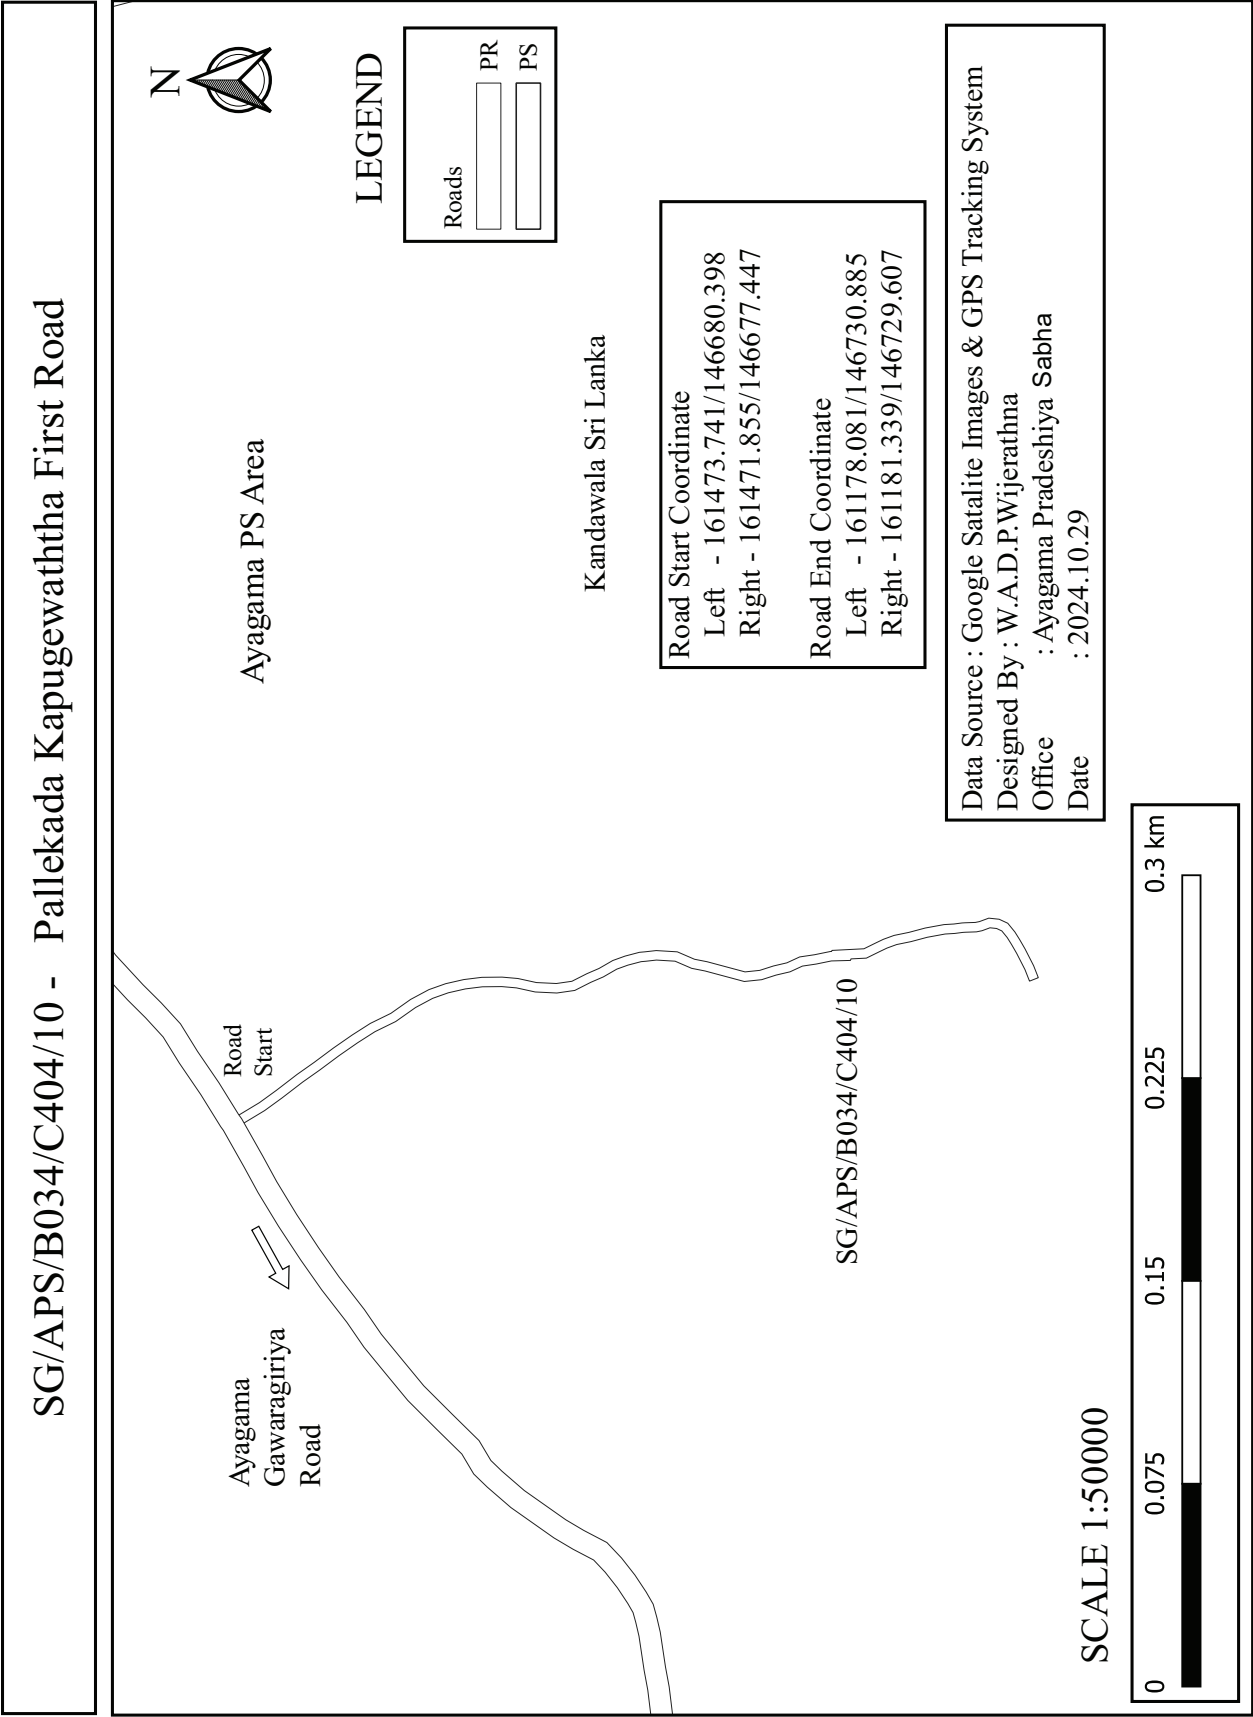

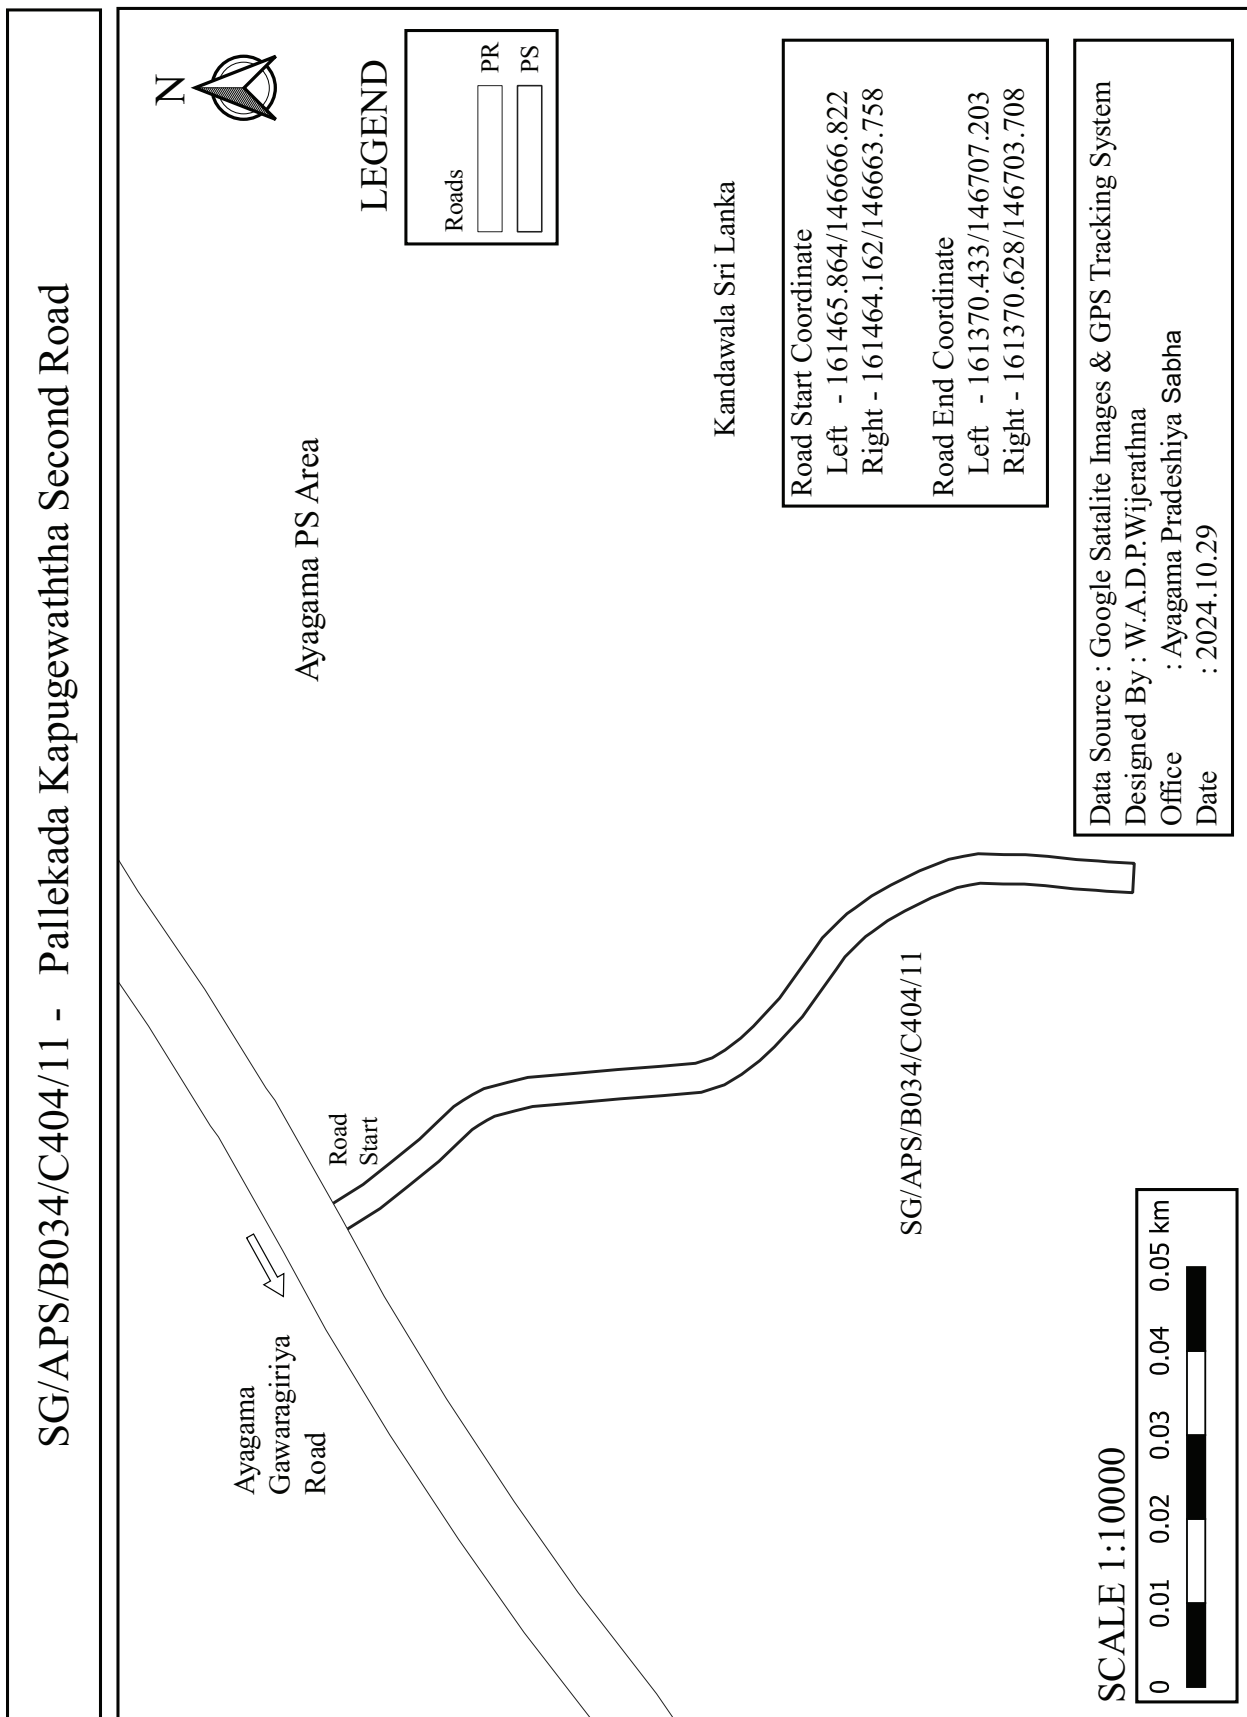

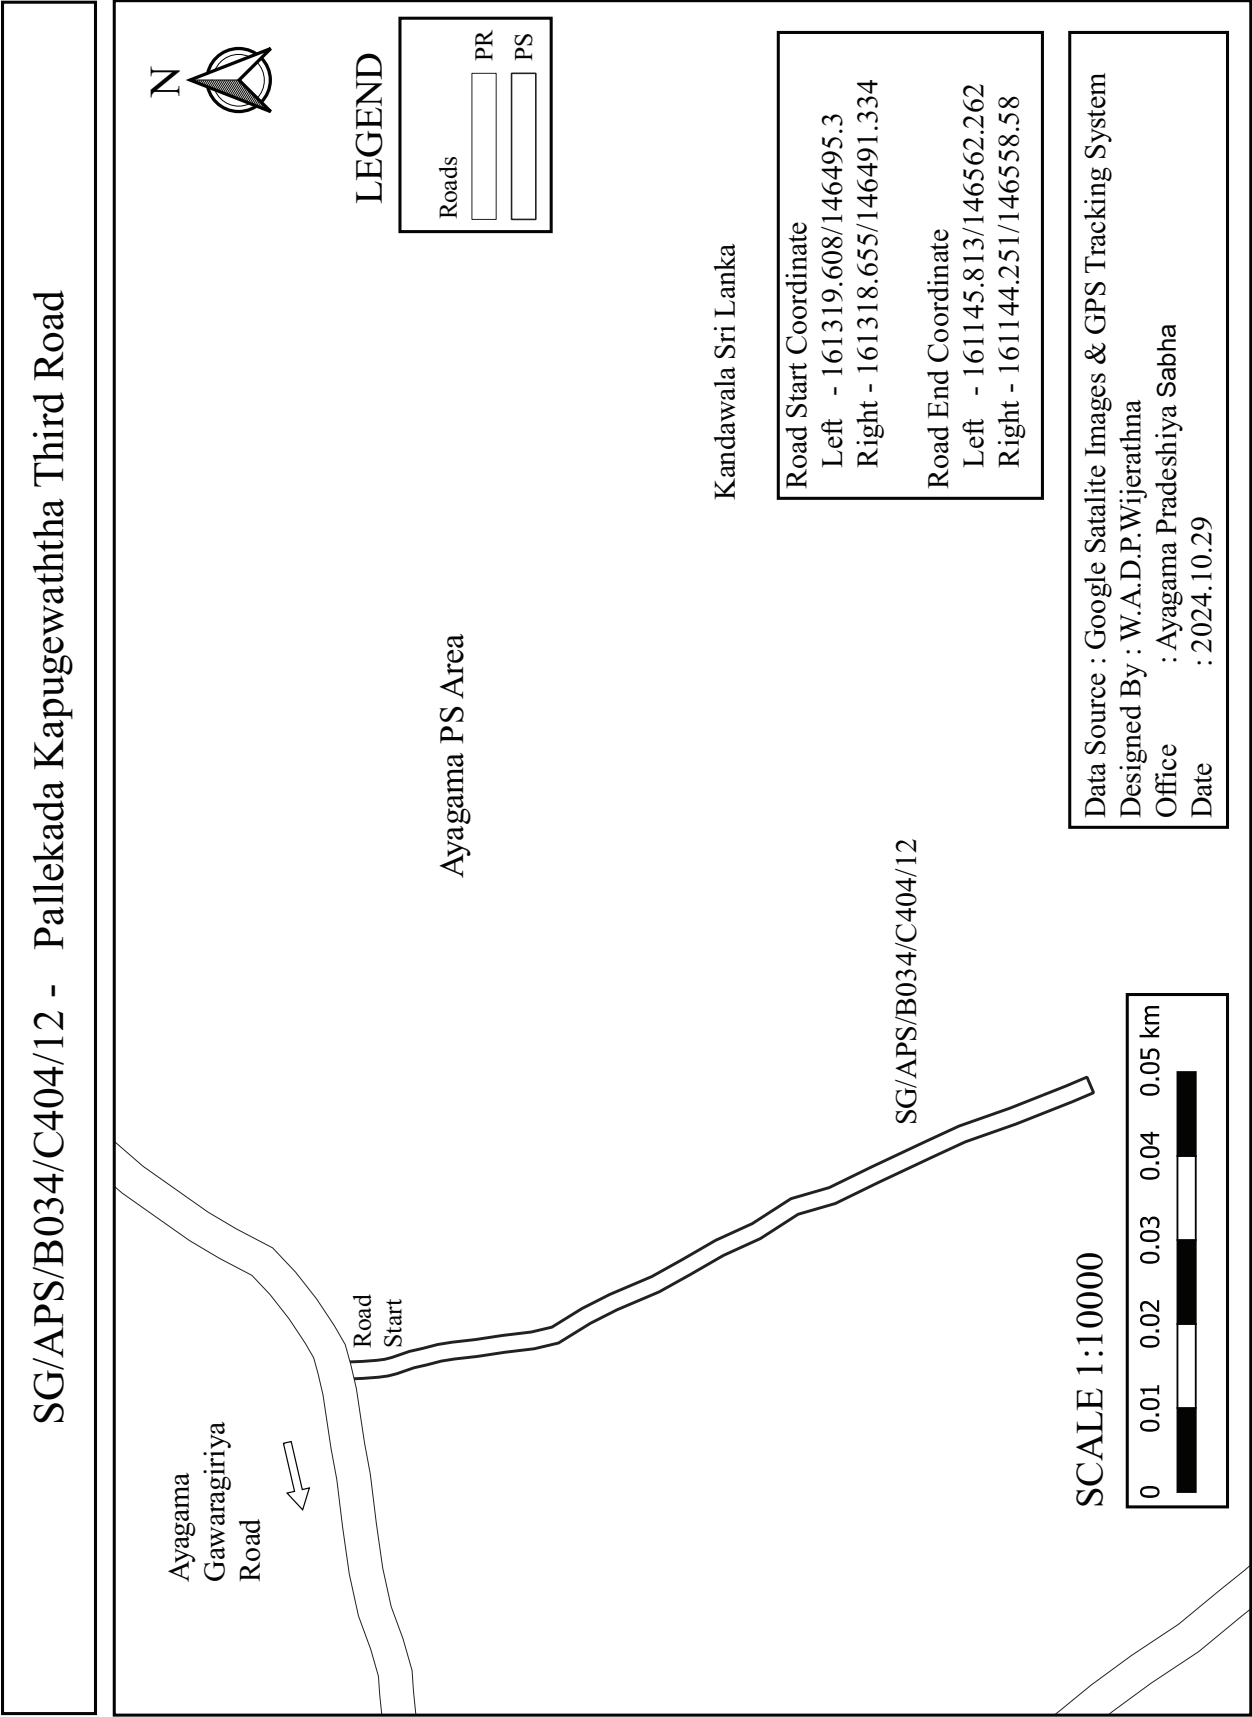

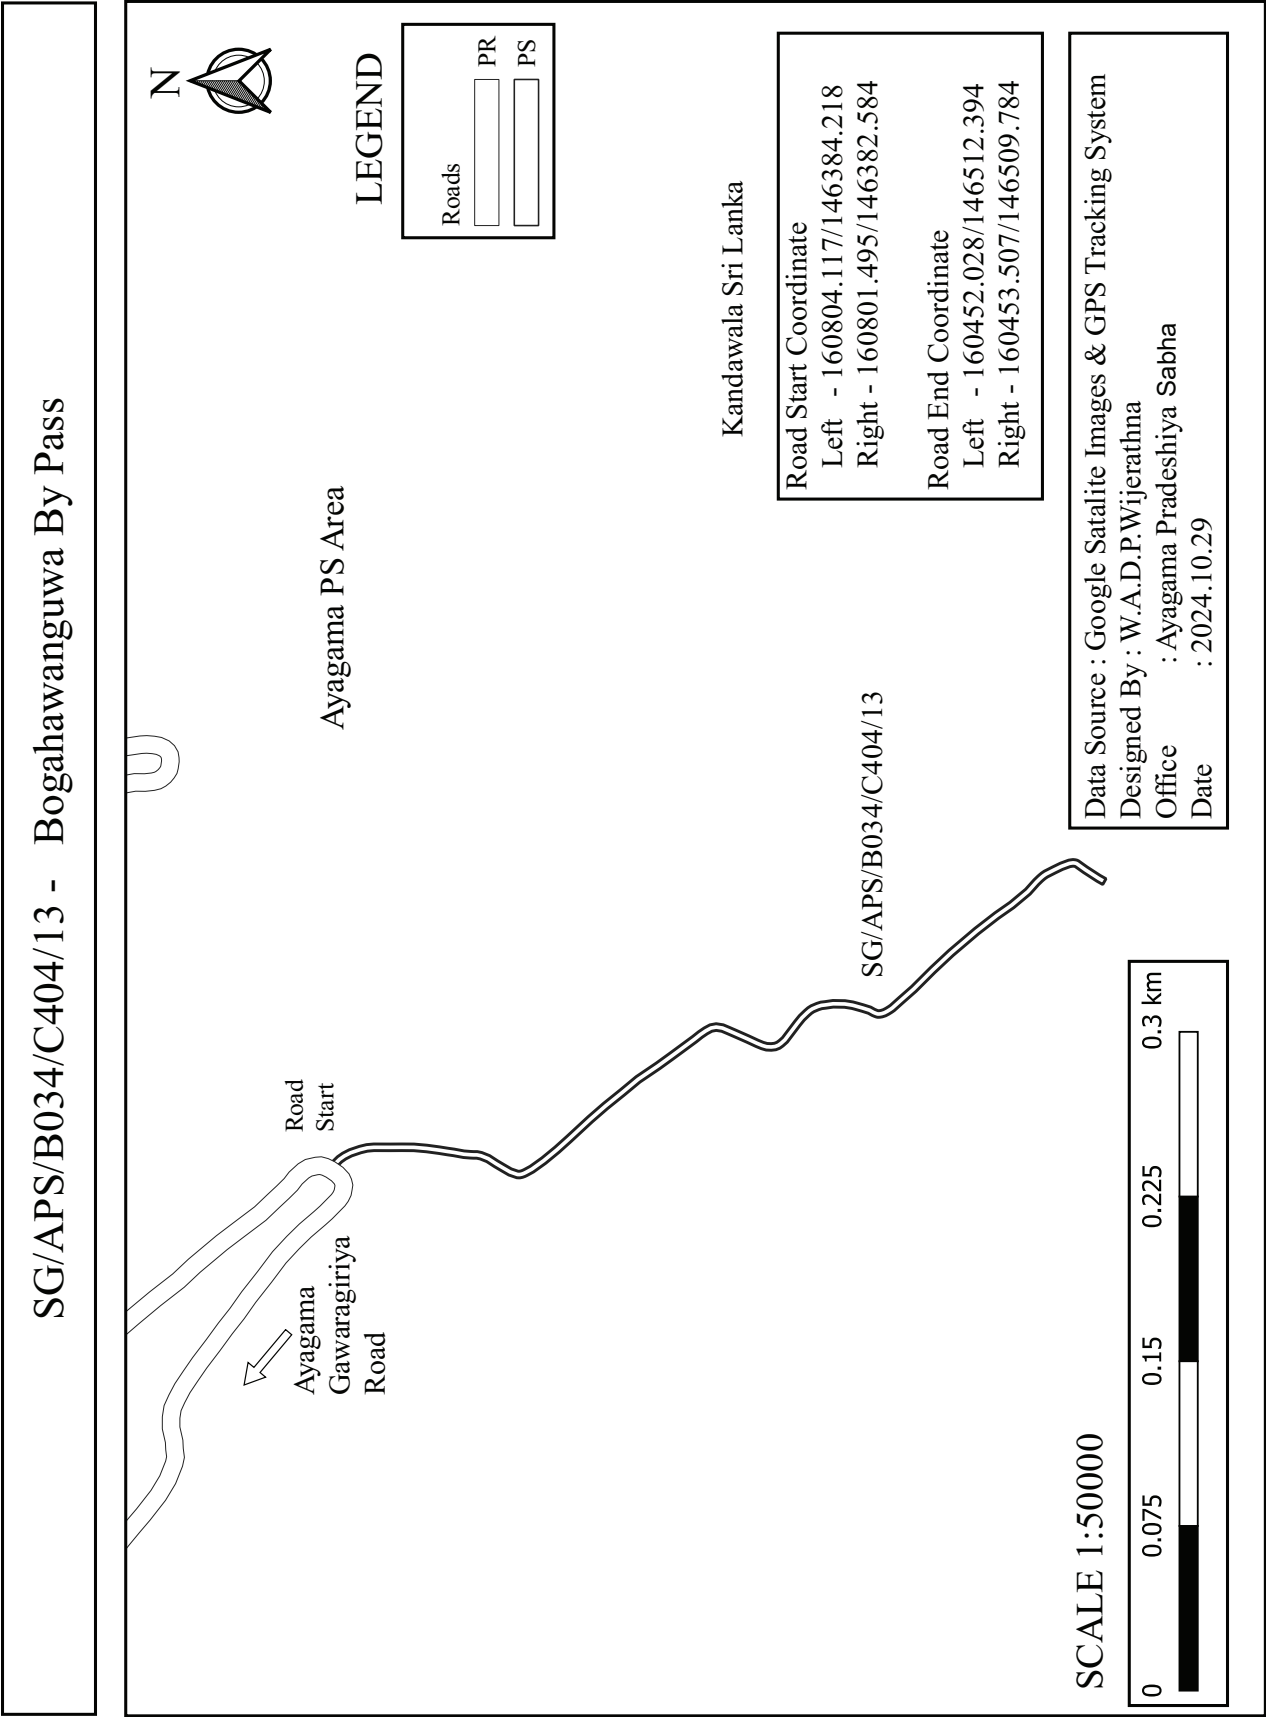

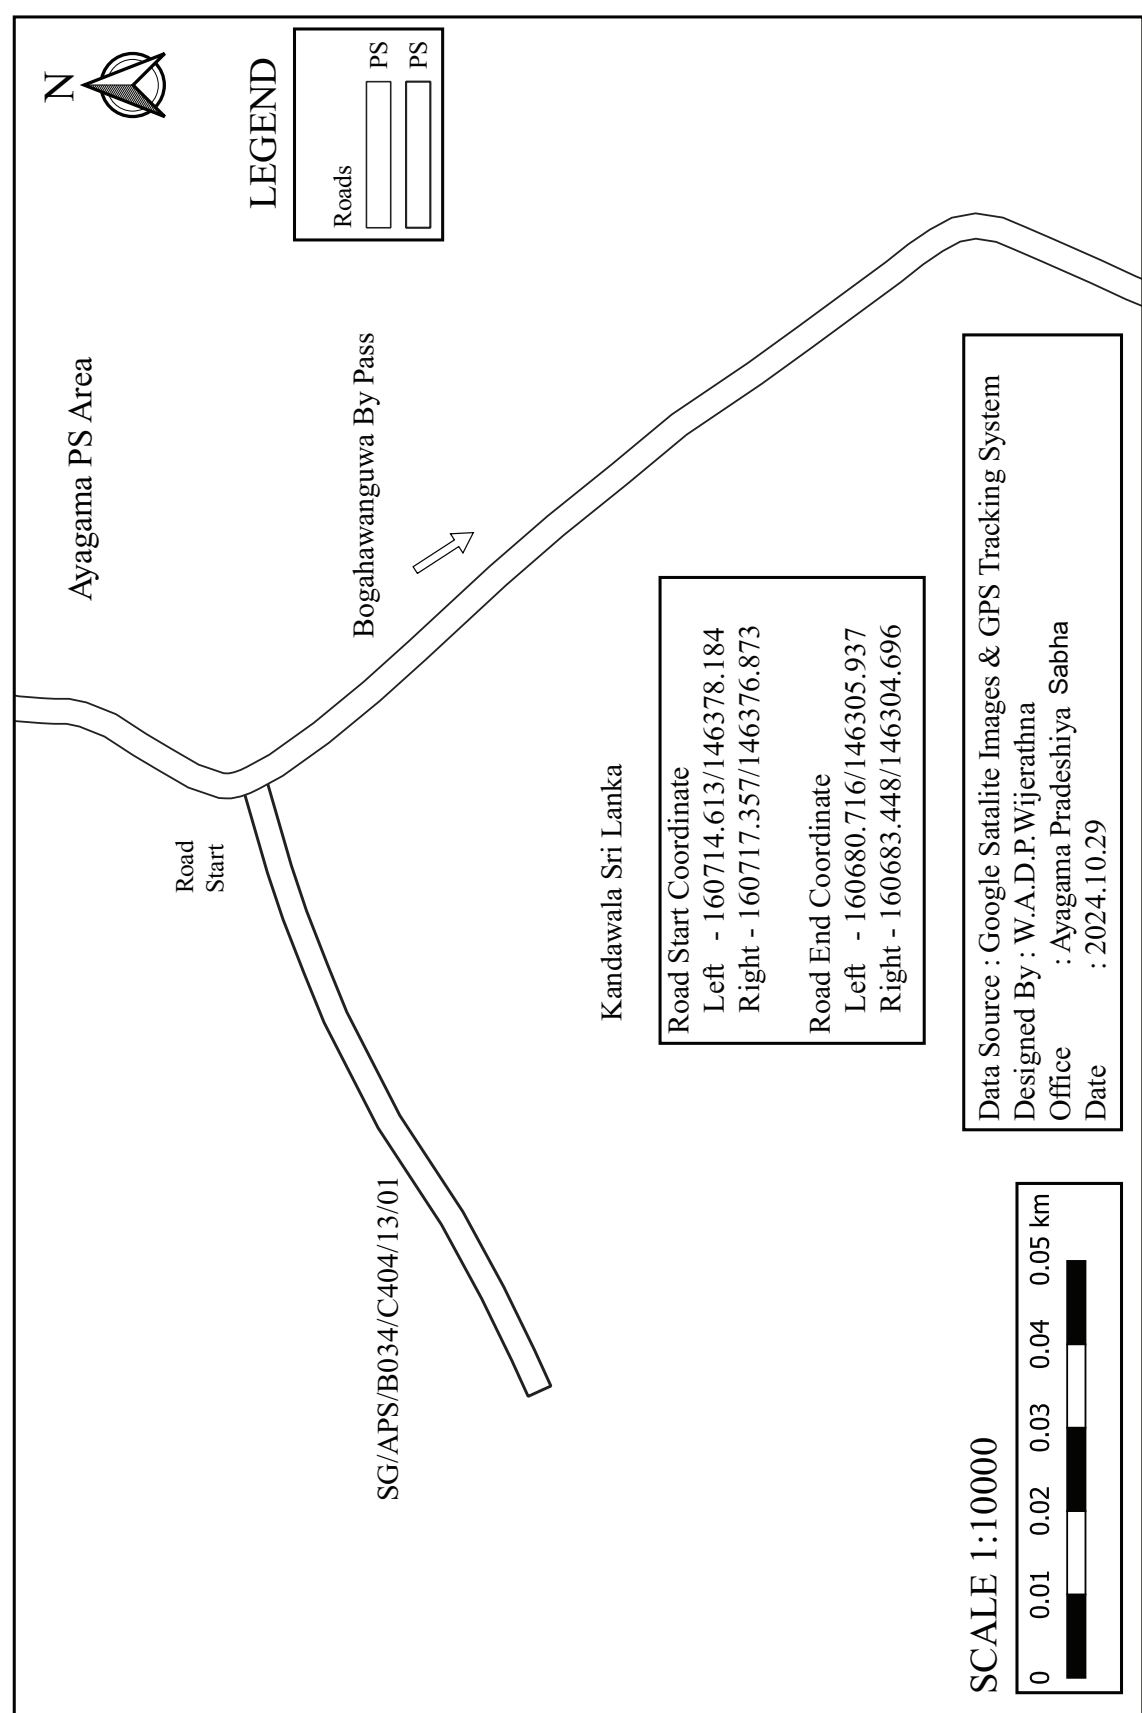

SG/APS/B034/C404/13/02 - Second Lane of Bogahawela

Kandawala Sri Lanka

Road Start Coordinate

Left - 160663.341/146420.705

Right - 160665.793/146418.821

Road End Coordinate

Left - 160614.46/146365.428


Right - 160615.045/146362.485

Ayagama PS Area



LEGEND

Roads

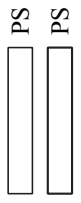

SG/APS/B034/C404/13/02

Road Start

Bogahawanguwa
By Pass




SCALE 1:10000


0 0.01 0.02 0.03 0.04 0.05 km




Data Source : Google Satalite Images & GPS Tracking System
Designed By : W.A.D.P.Wijerathna
Office : Ayagama Pradeshiya Sabha
Date : 2024.10.29

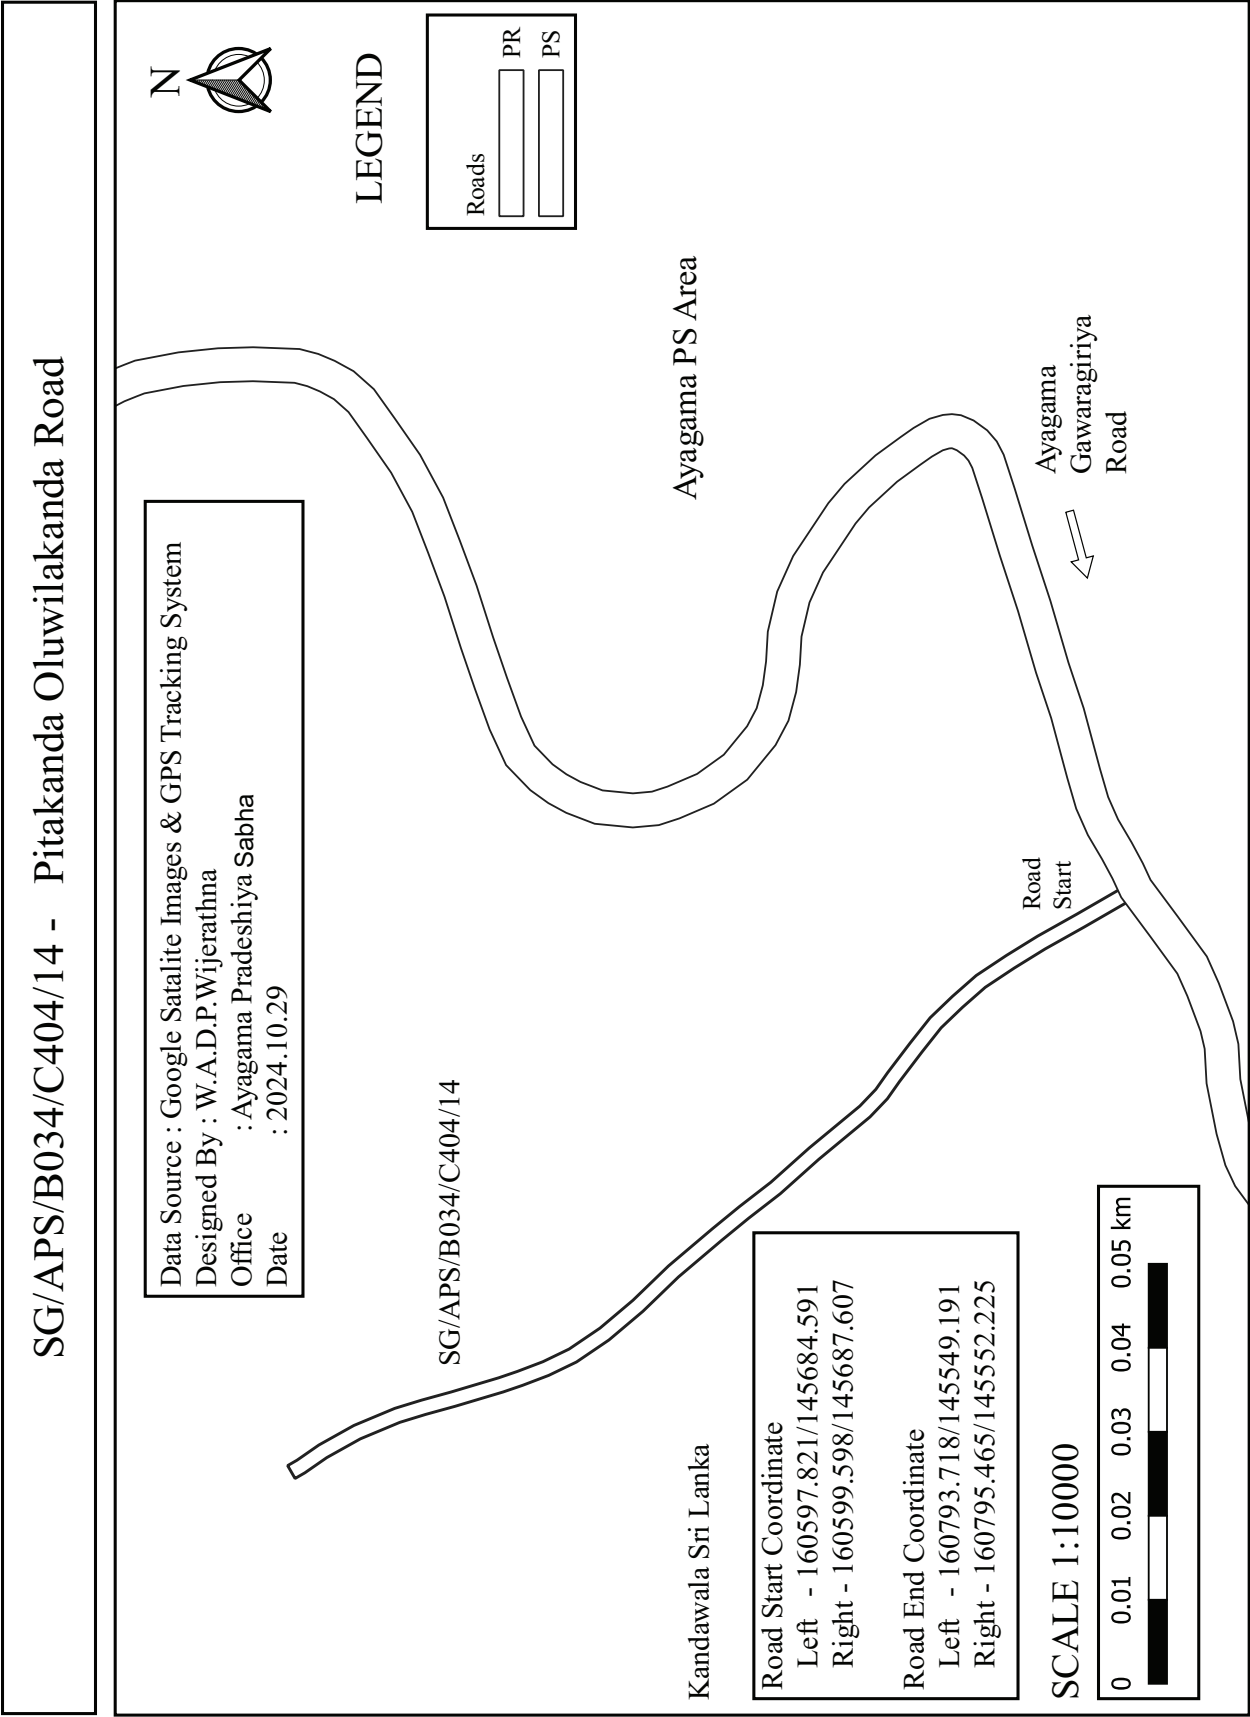



SG/APS/B034/C404/15 - Pitakanda Malgahahena Road

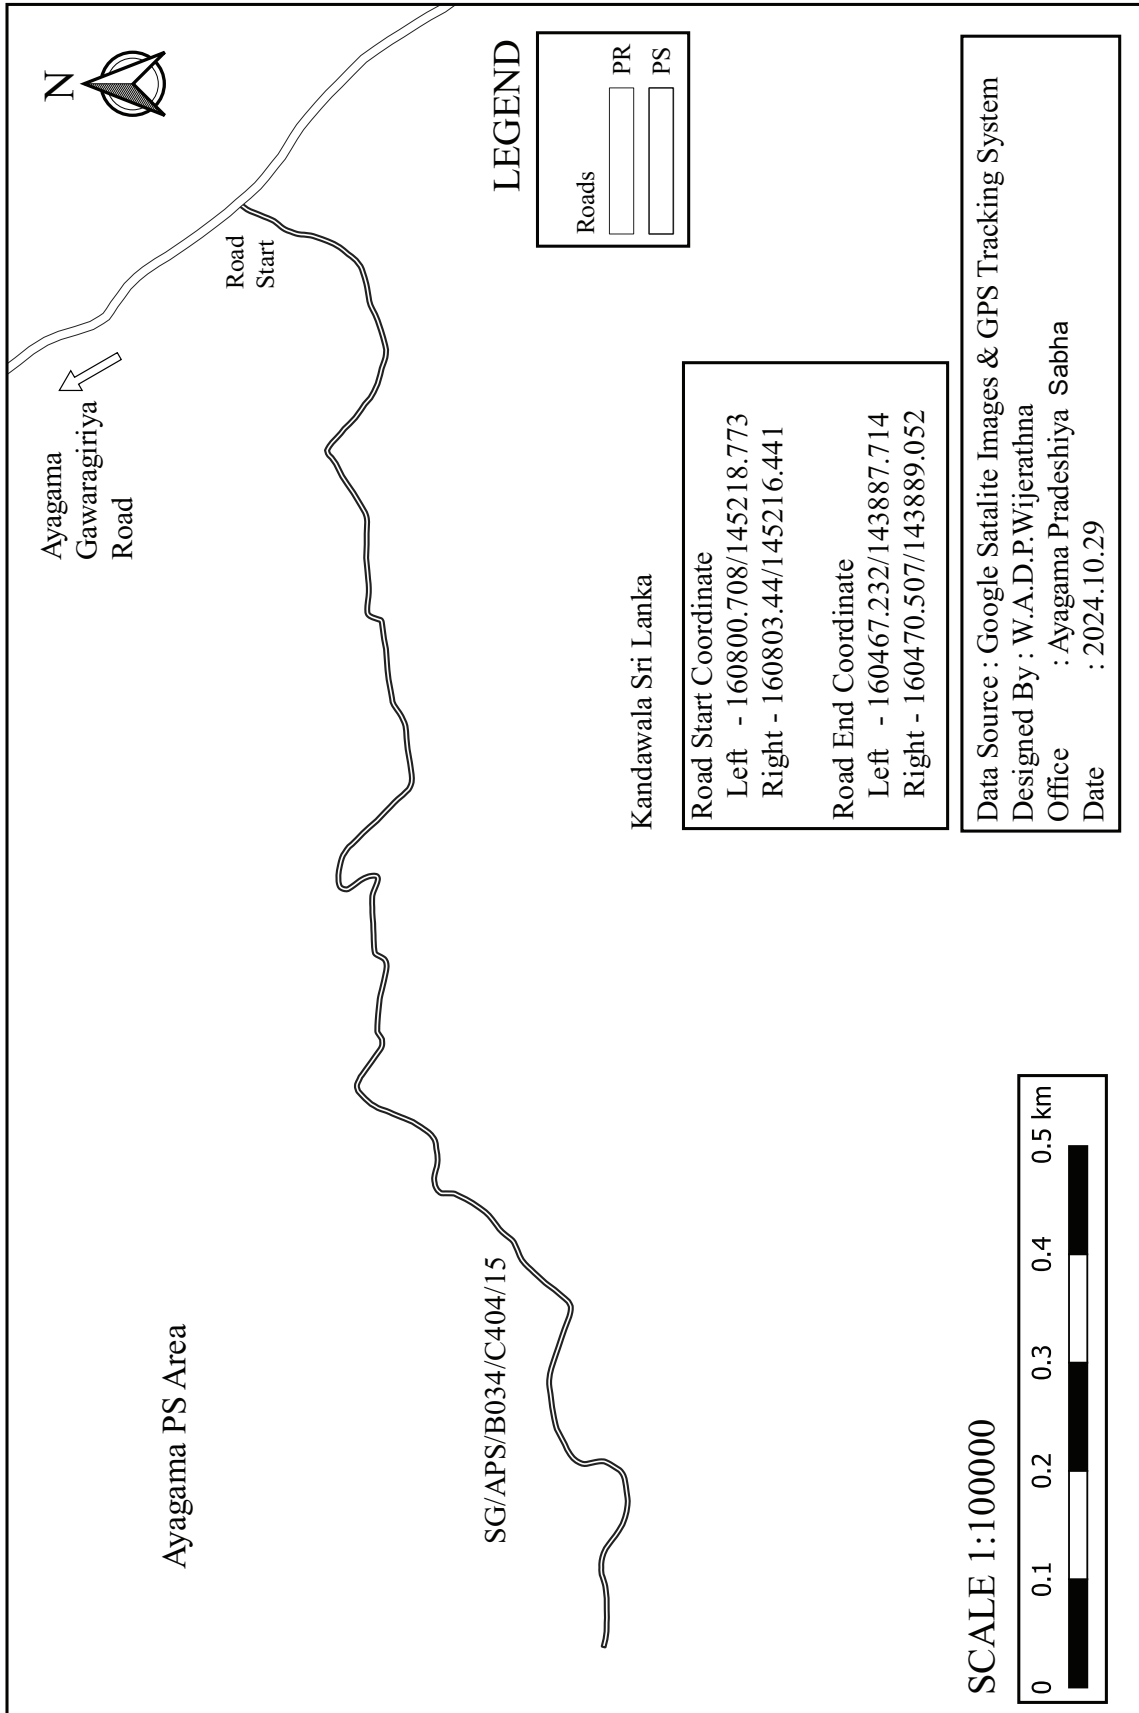


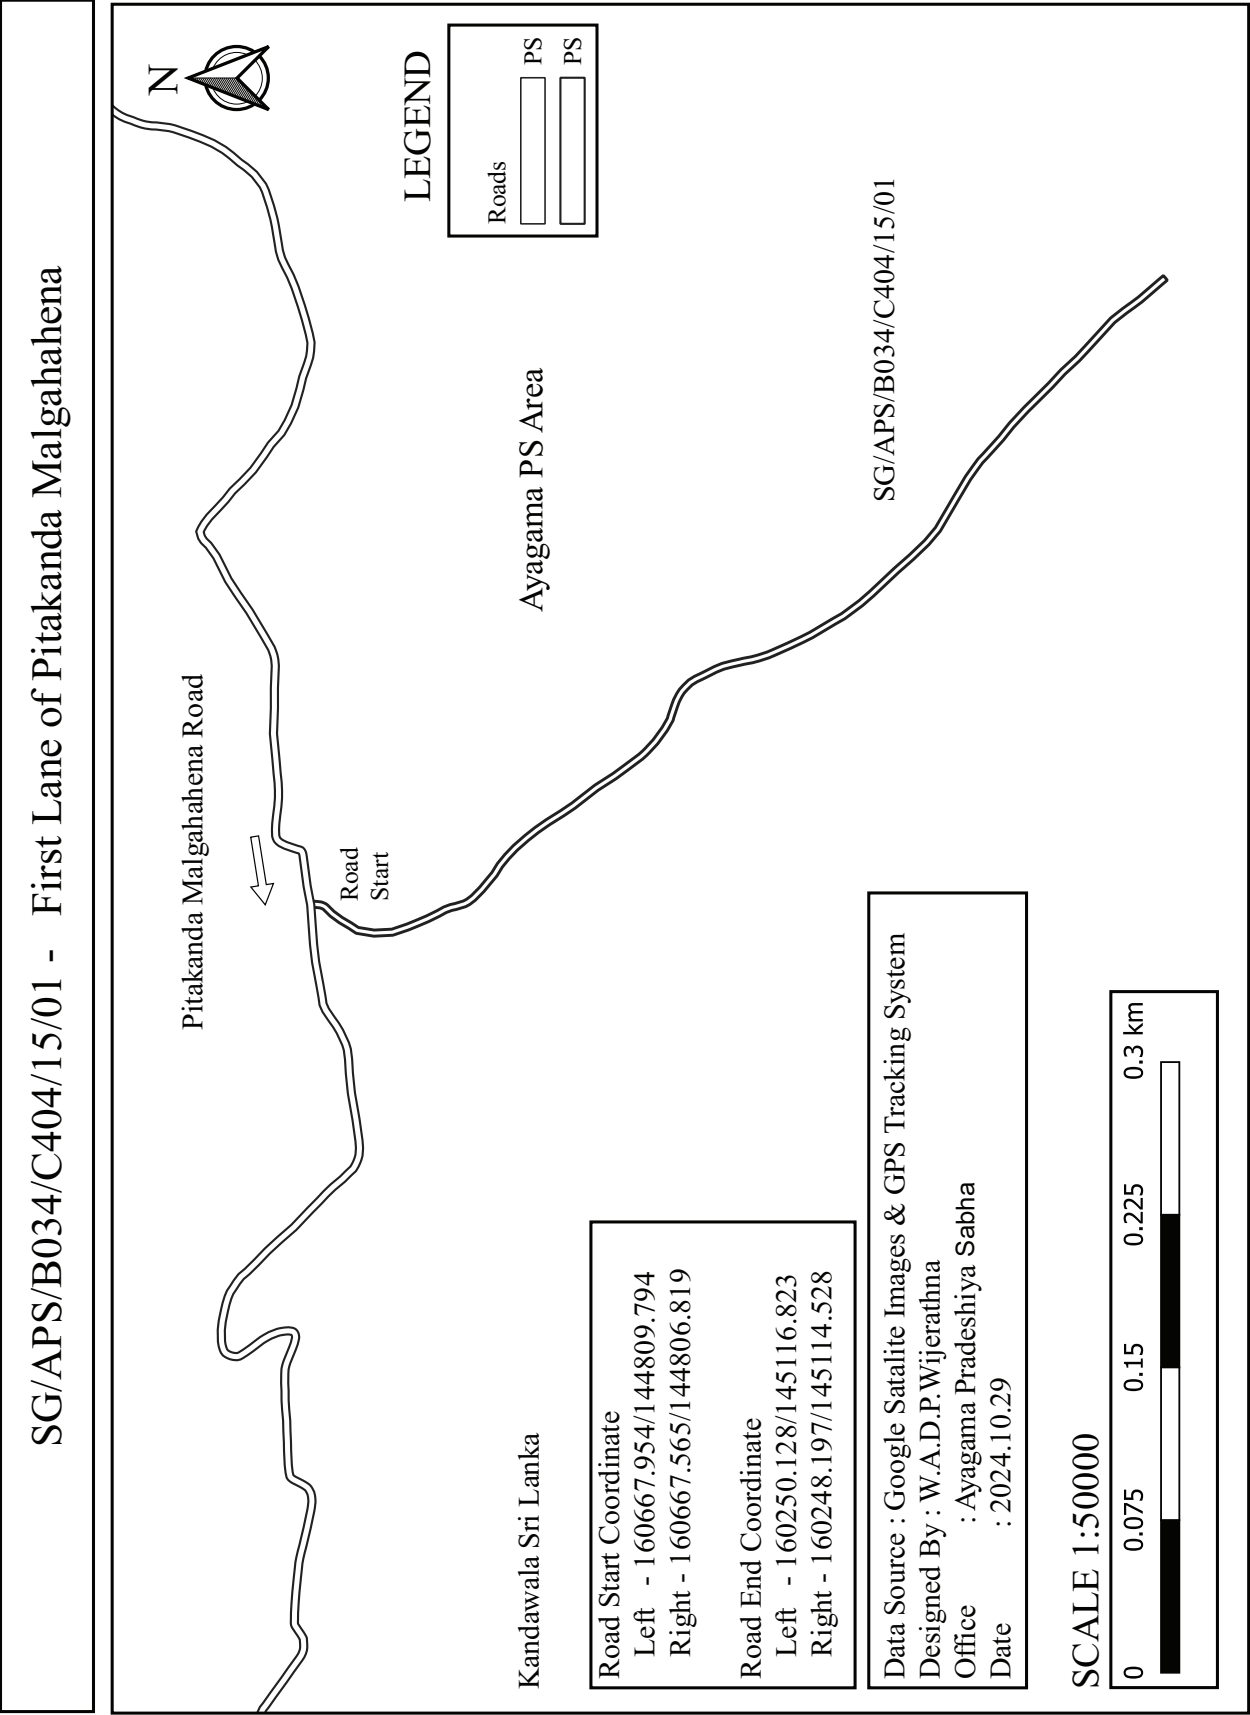


SG/APS/B034/C404/16 - First Lane of Gawaragiriya

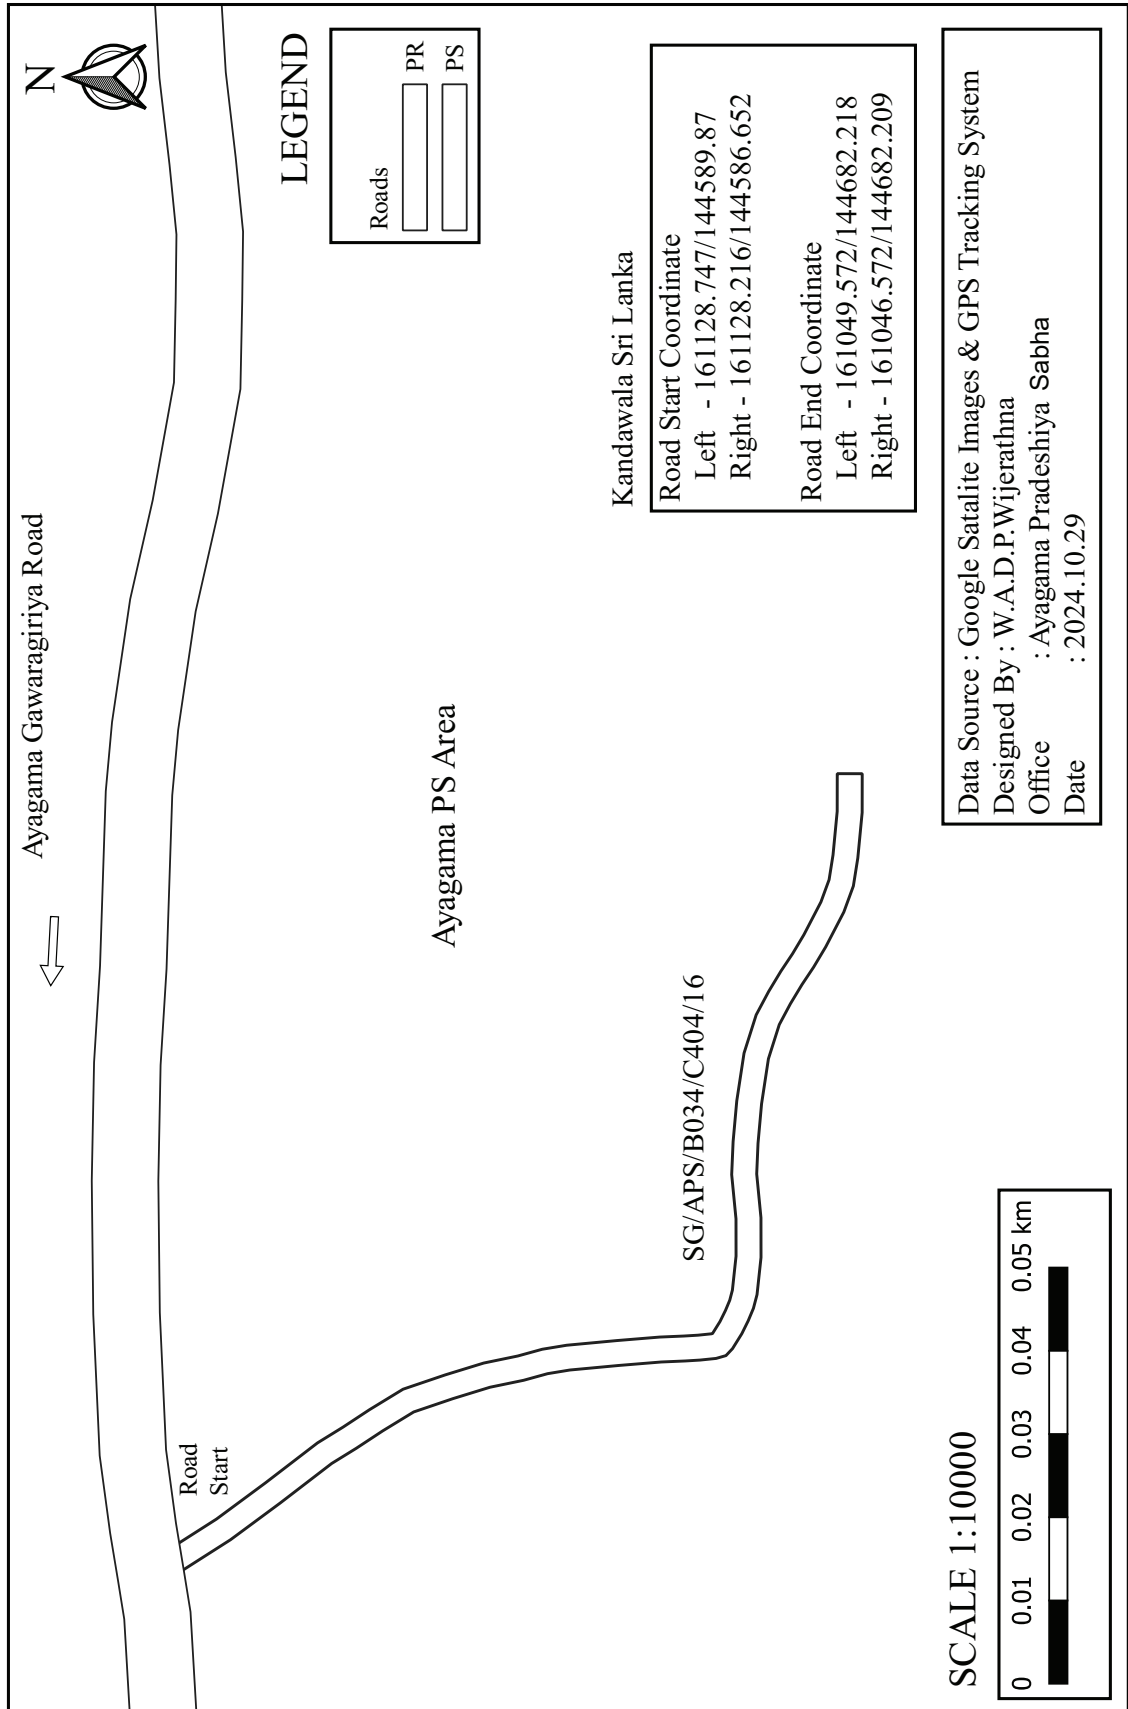


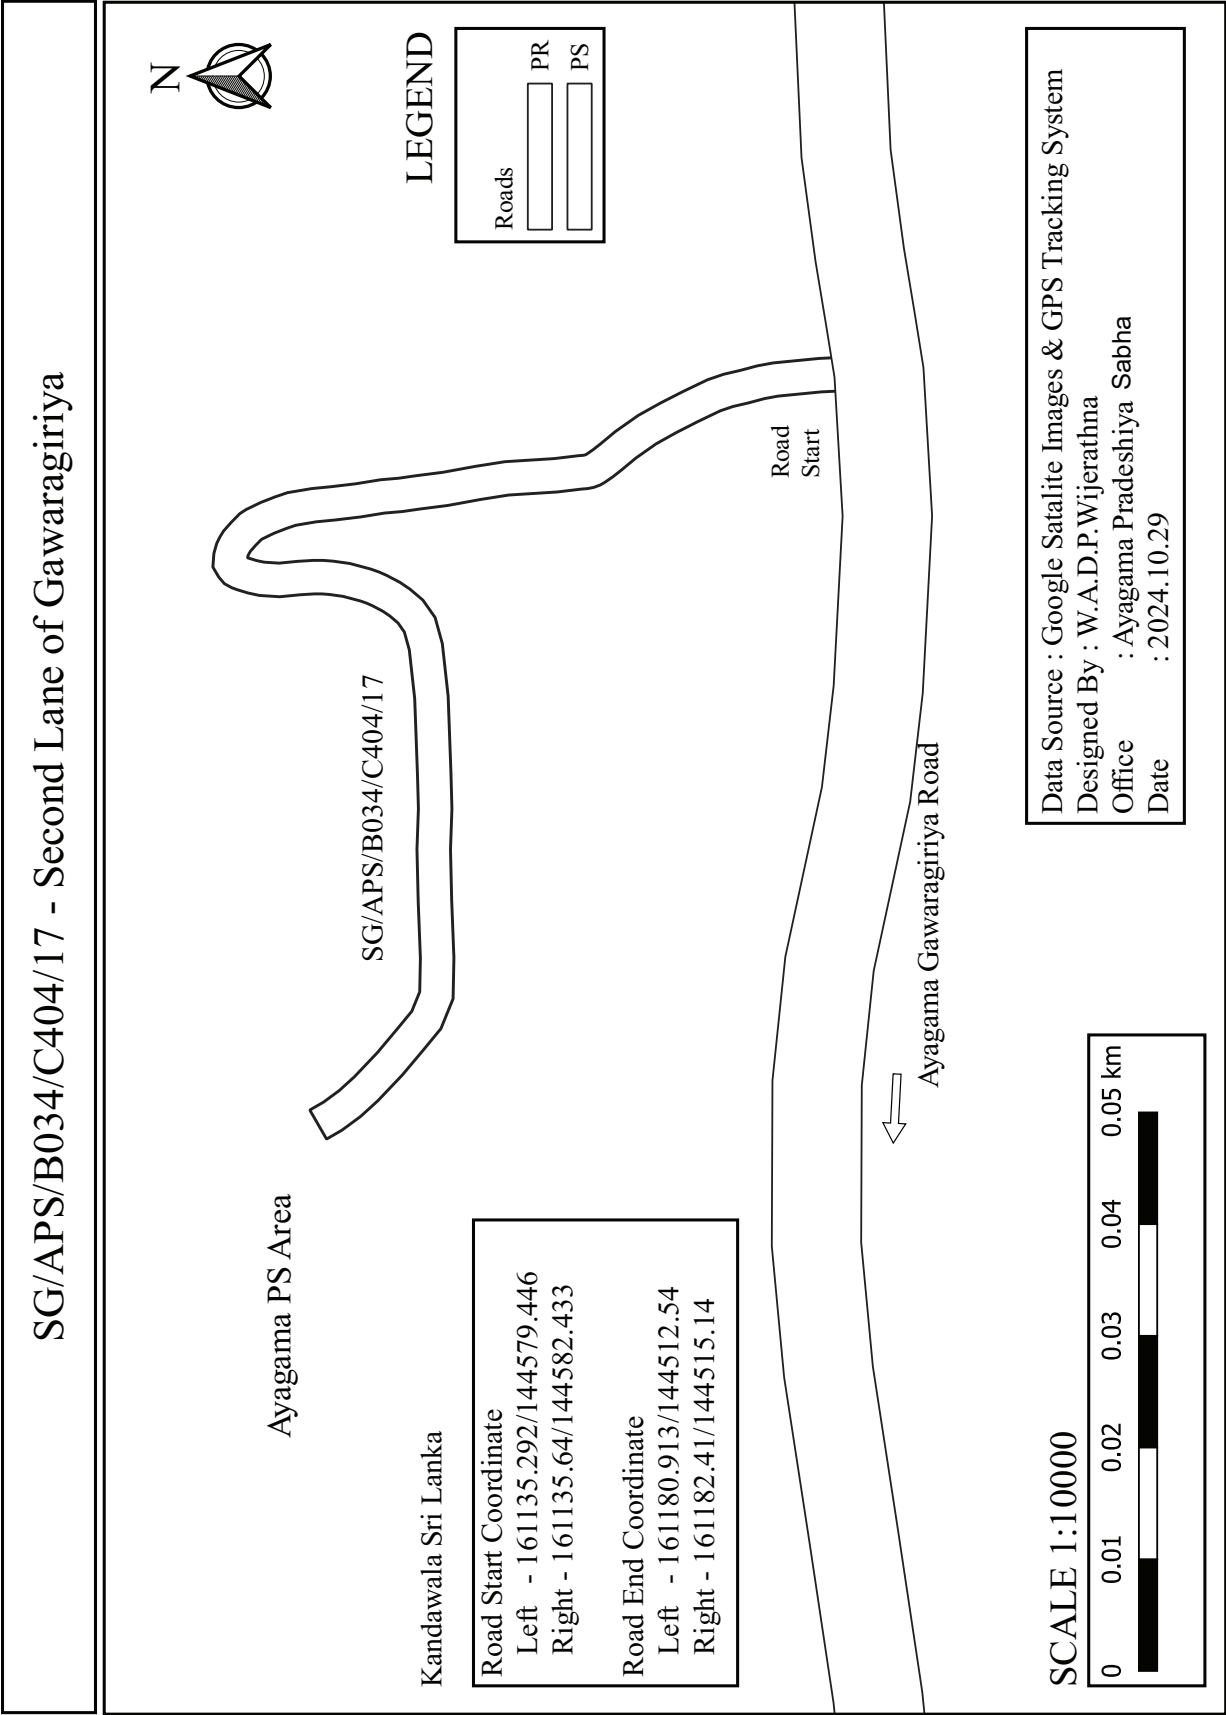


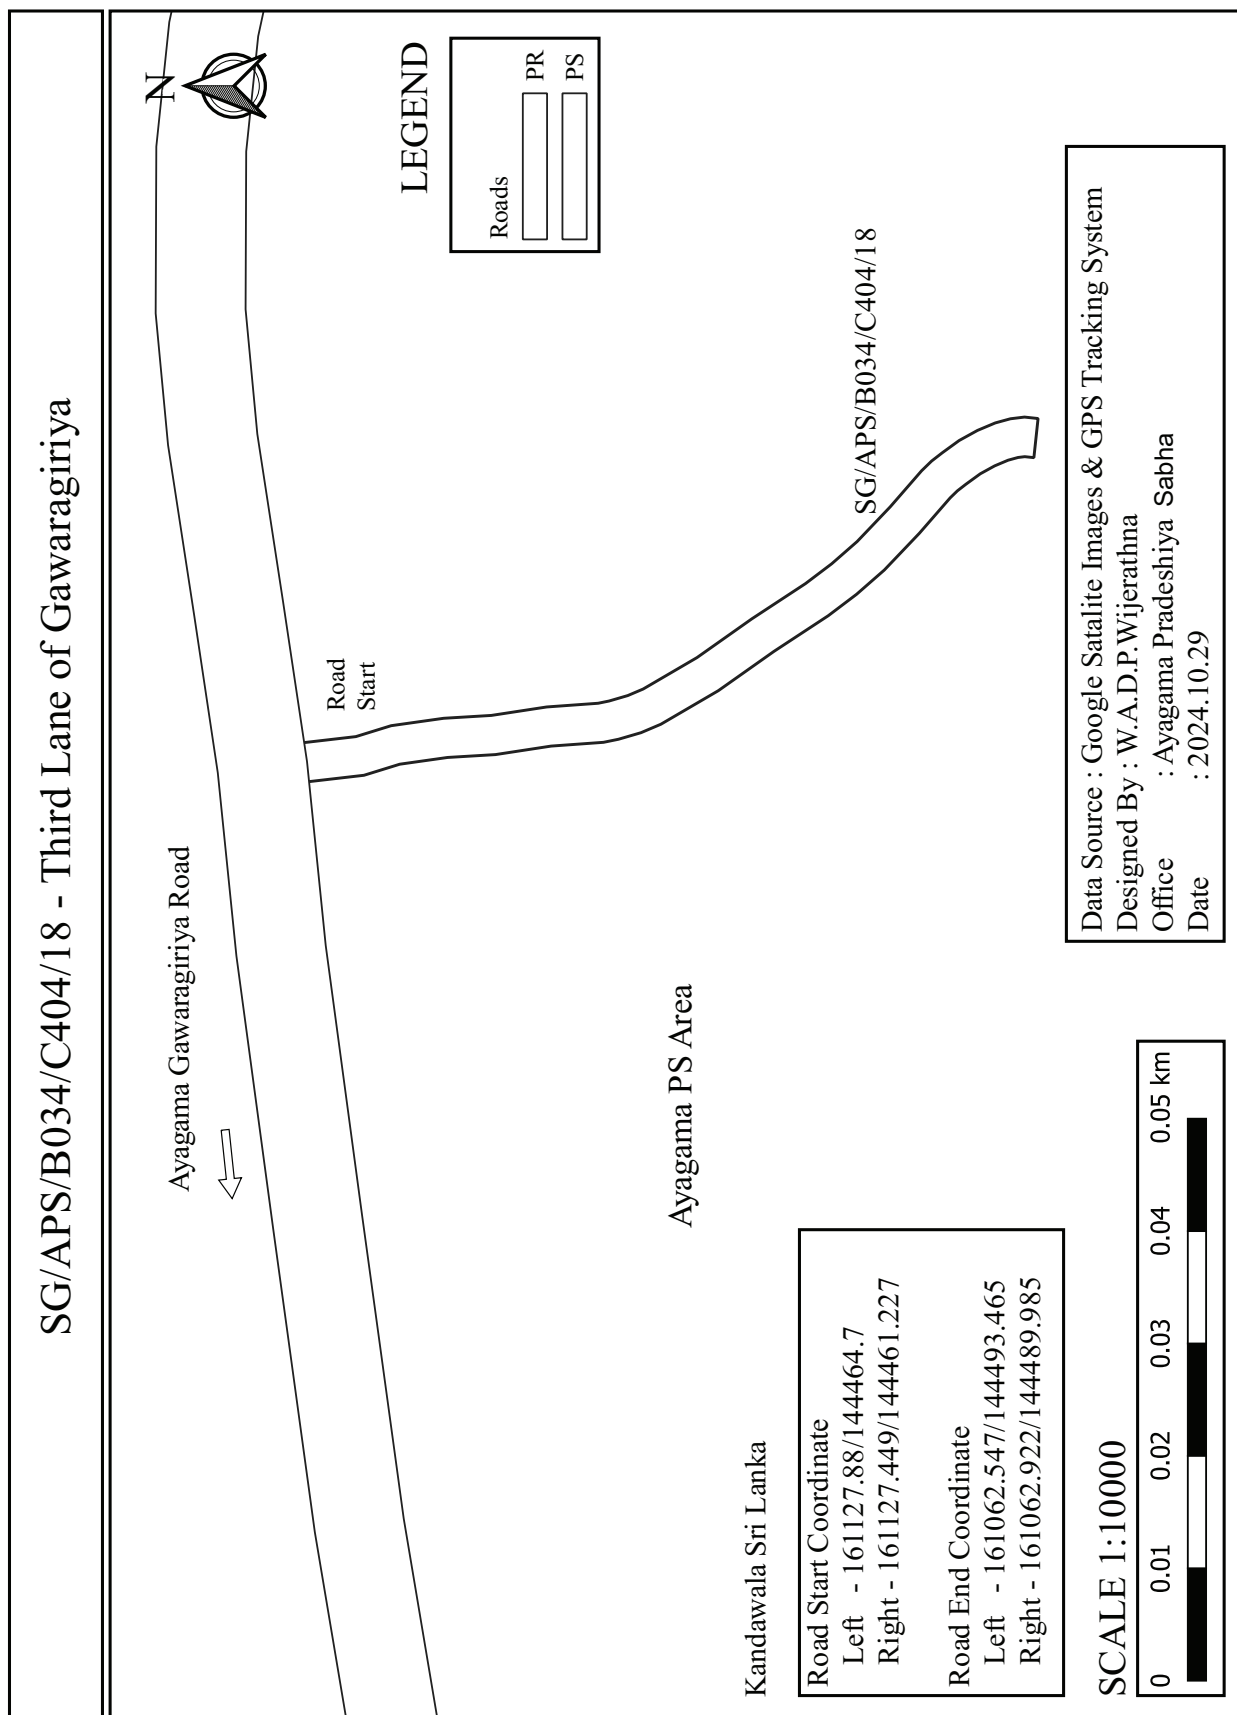


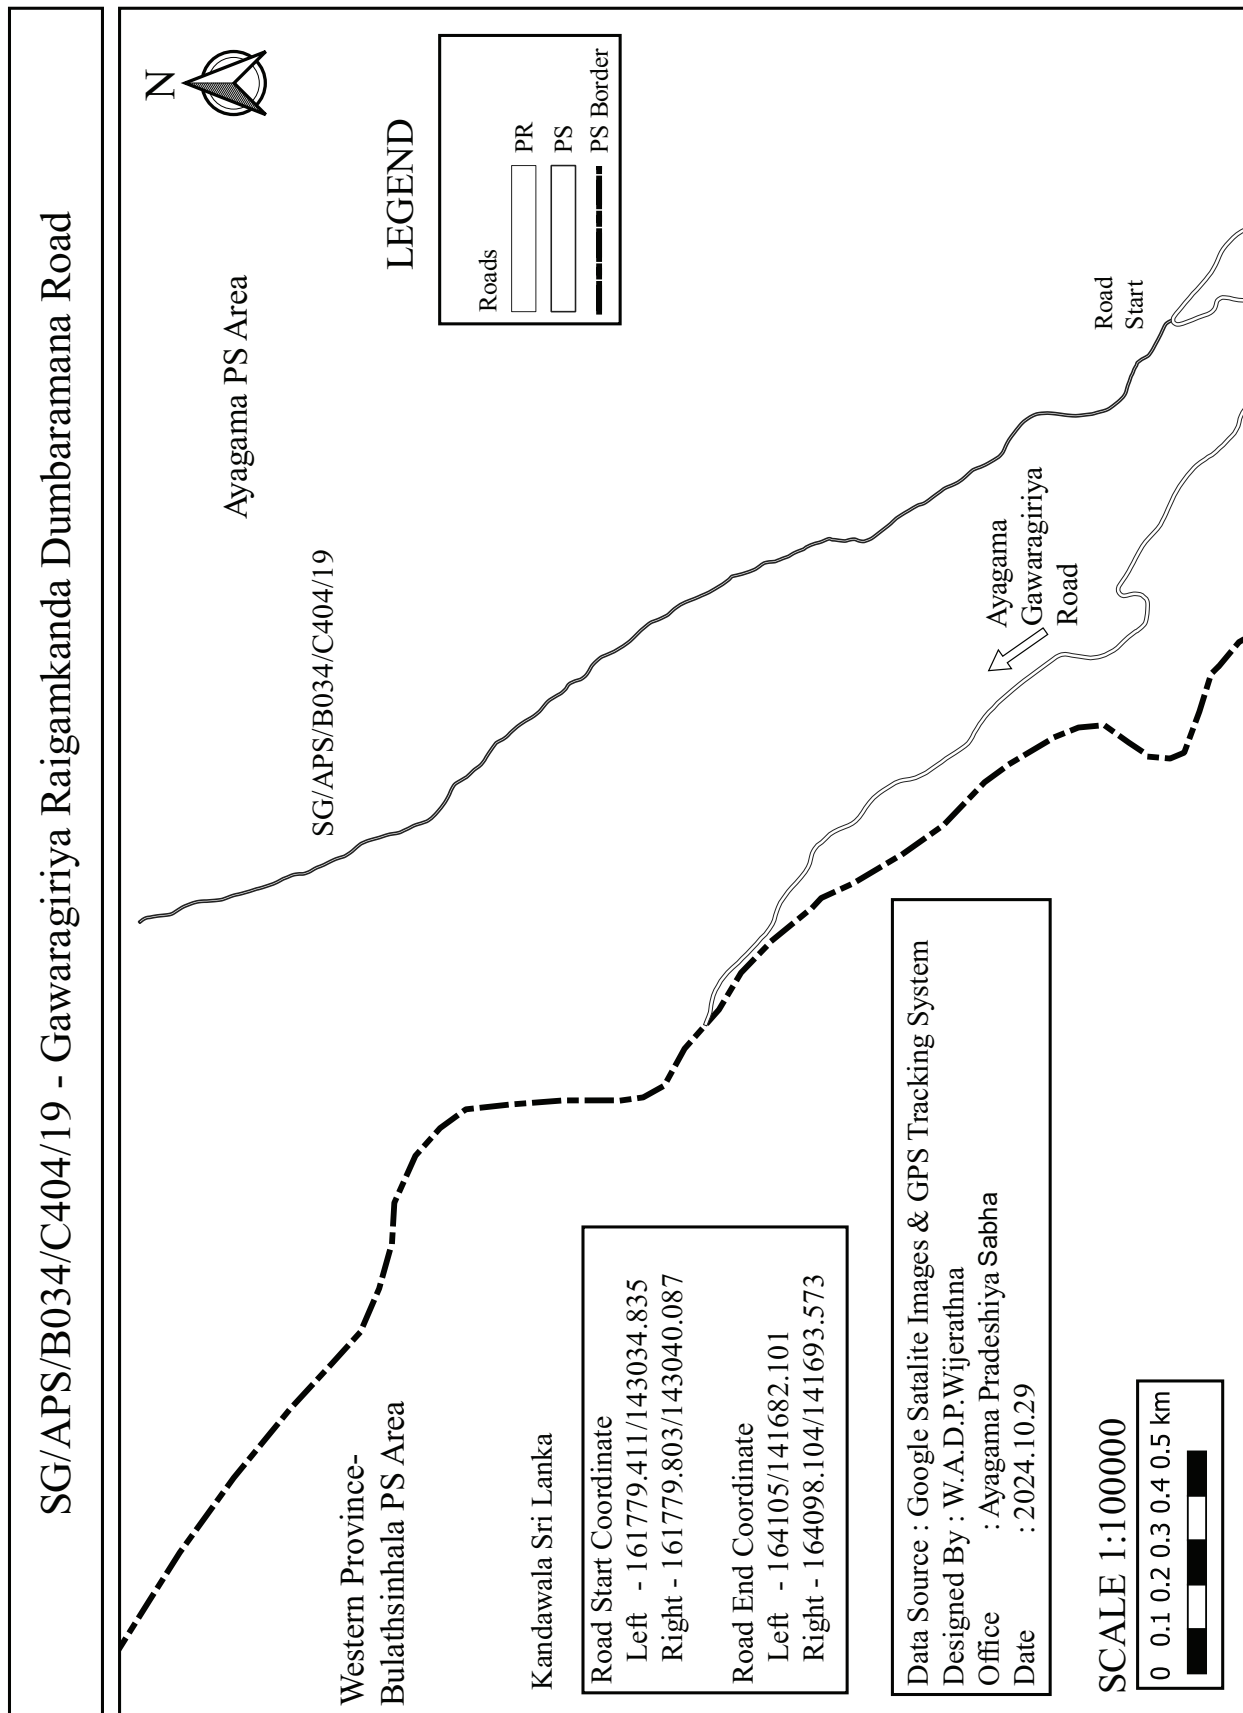


SG/APS/B034/C404/19/01 - First Lane of Raigamkanda

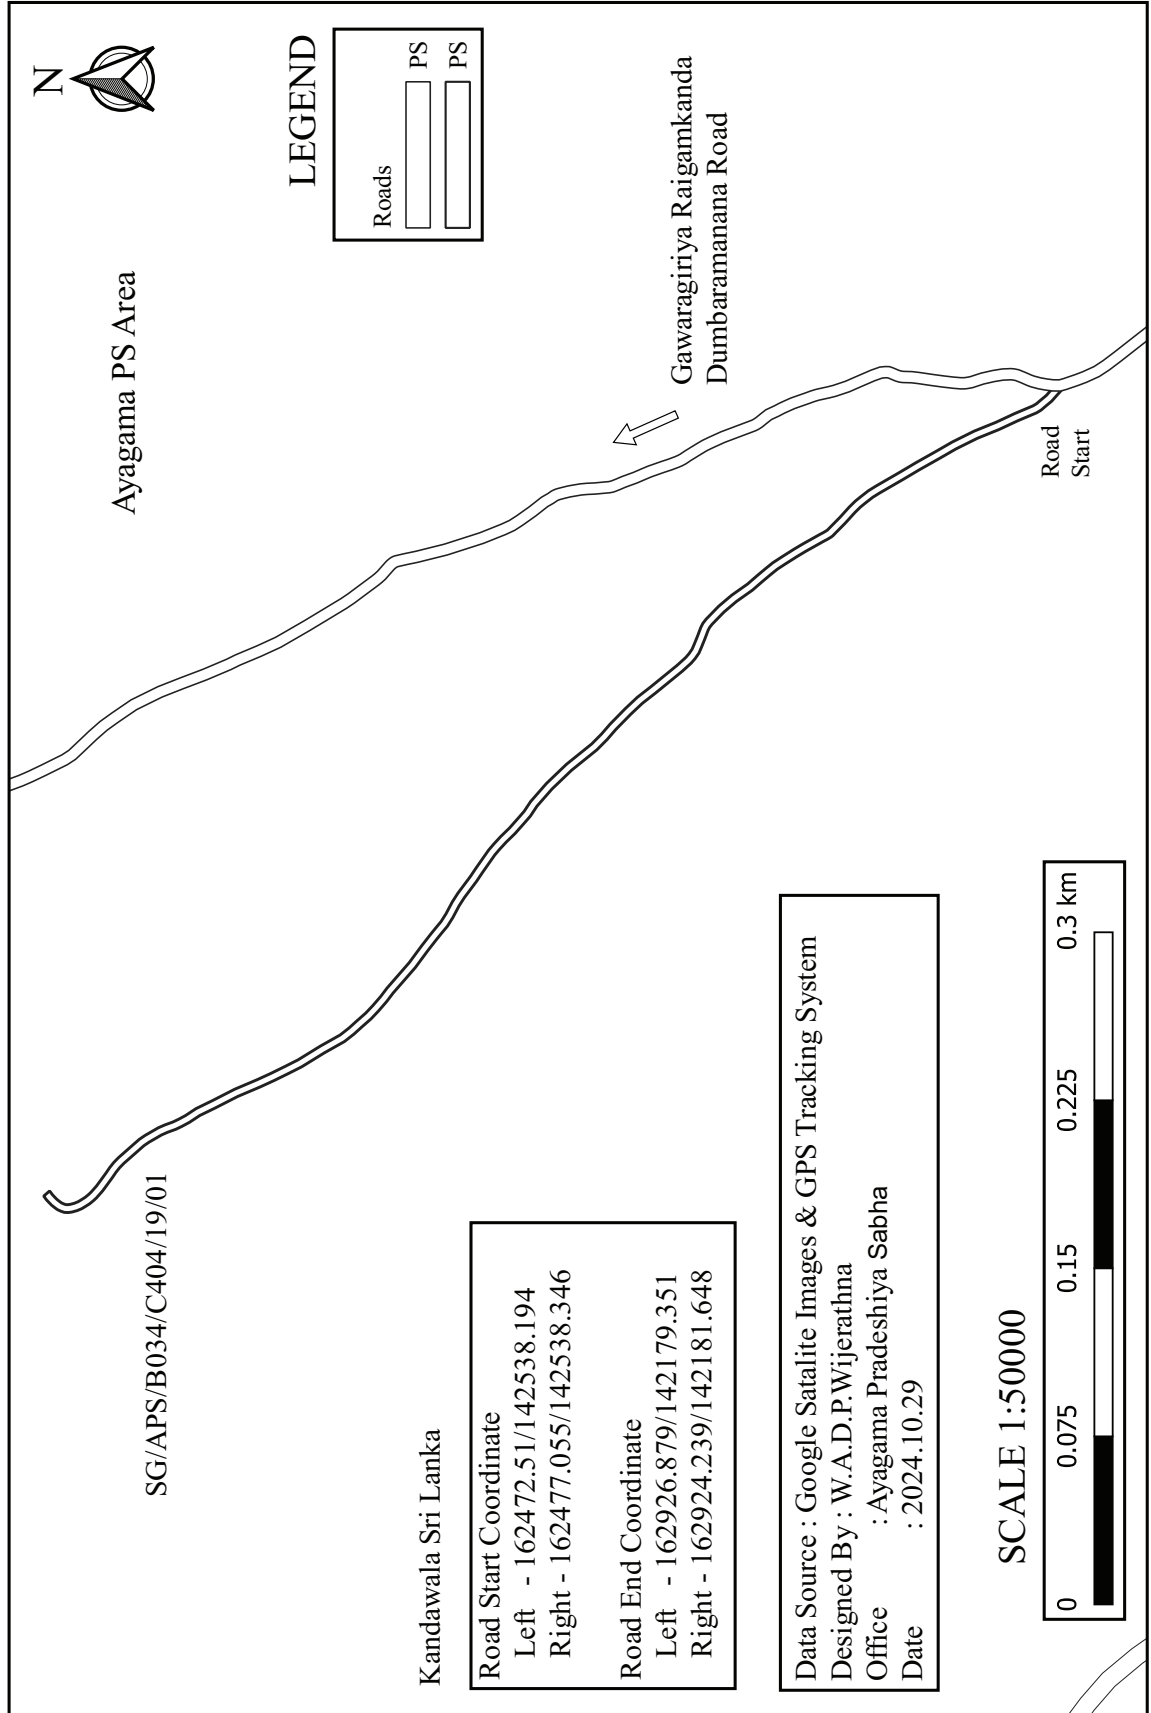


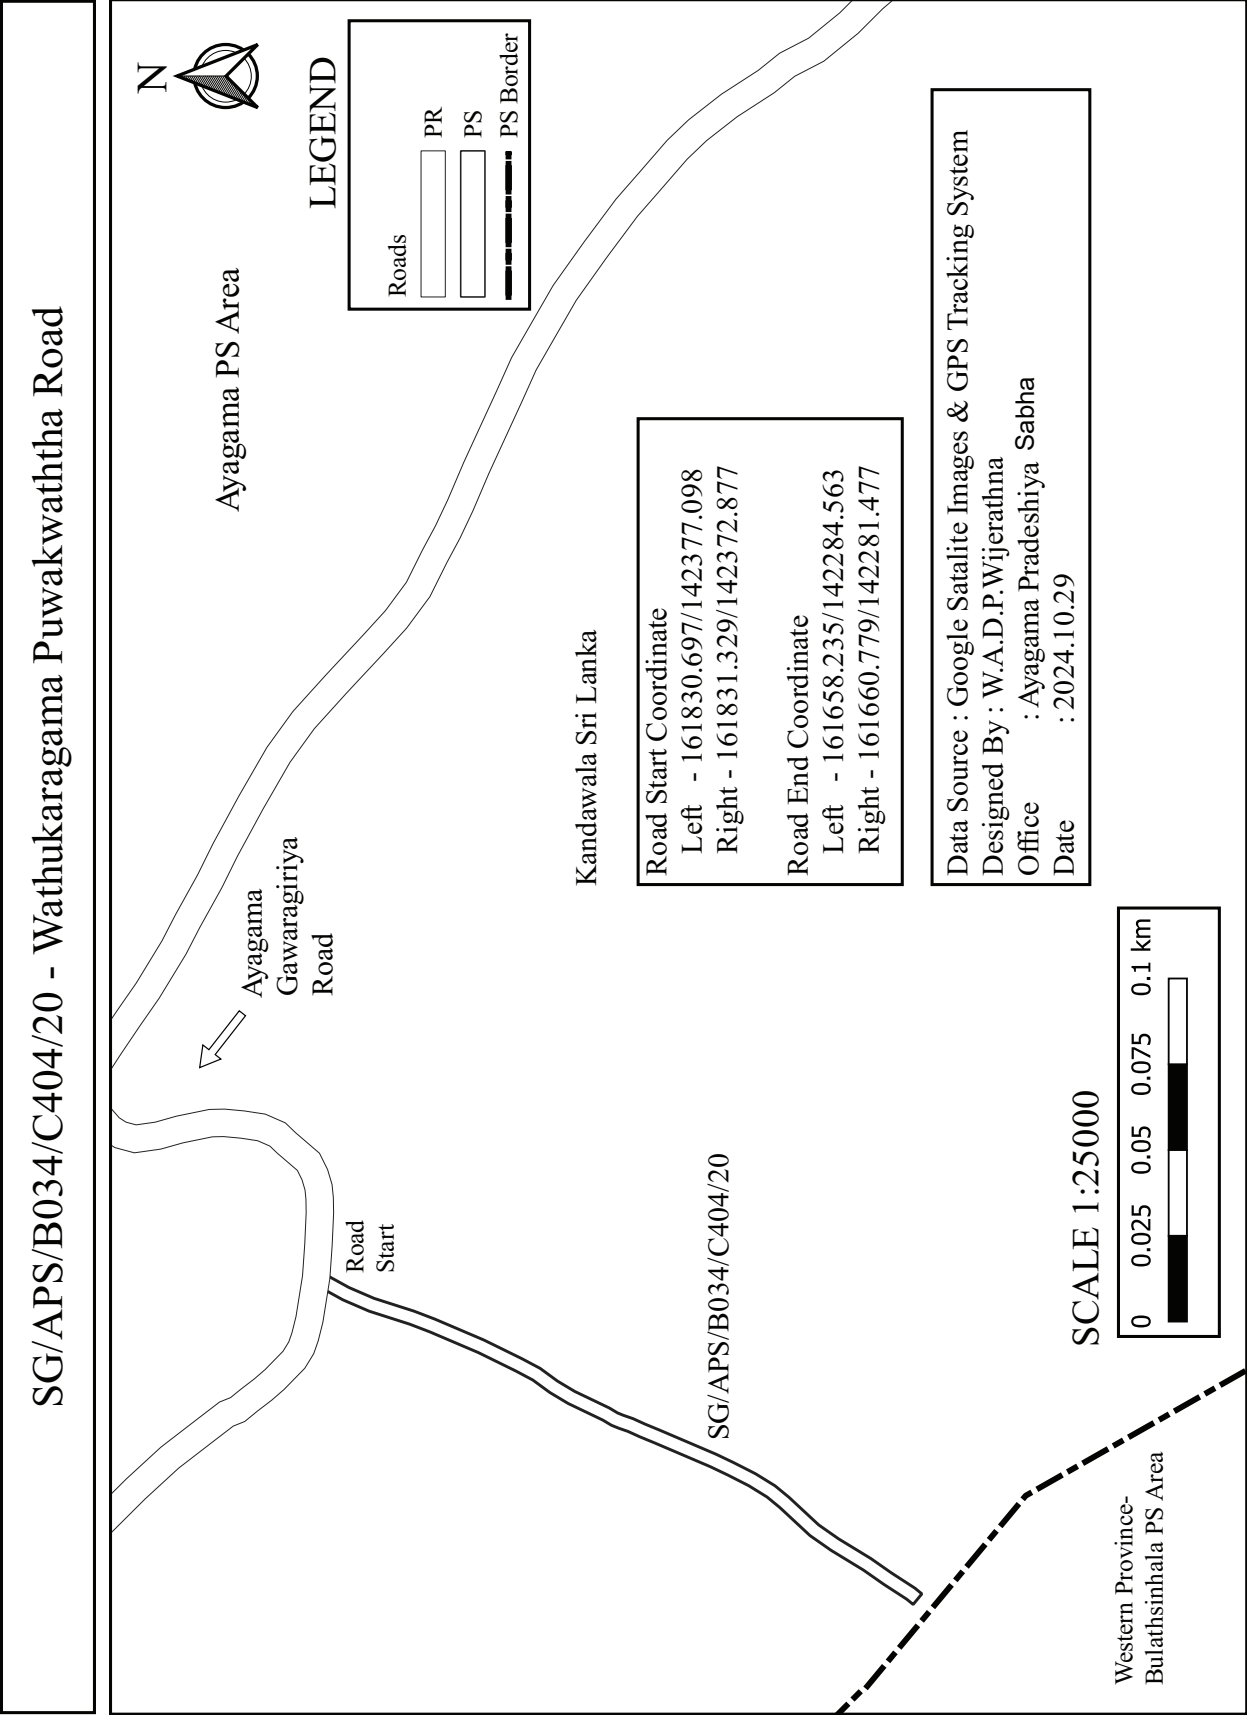


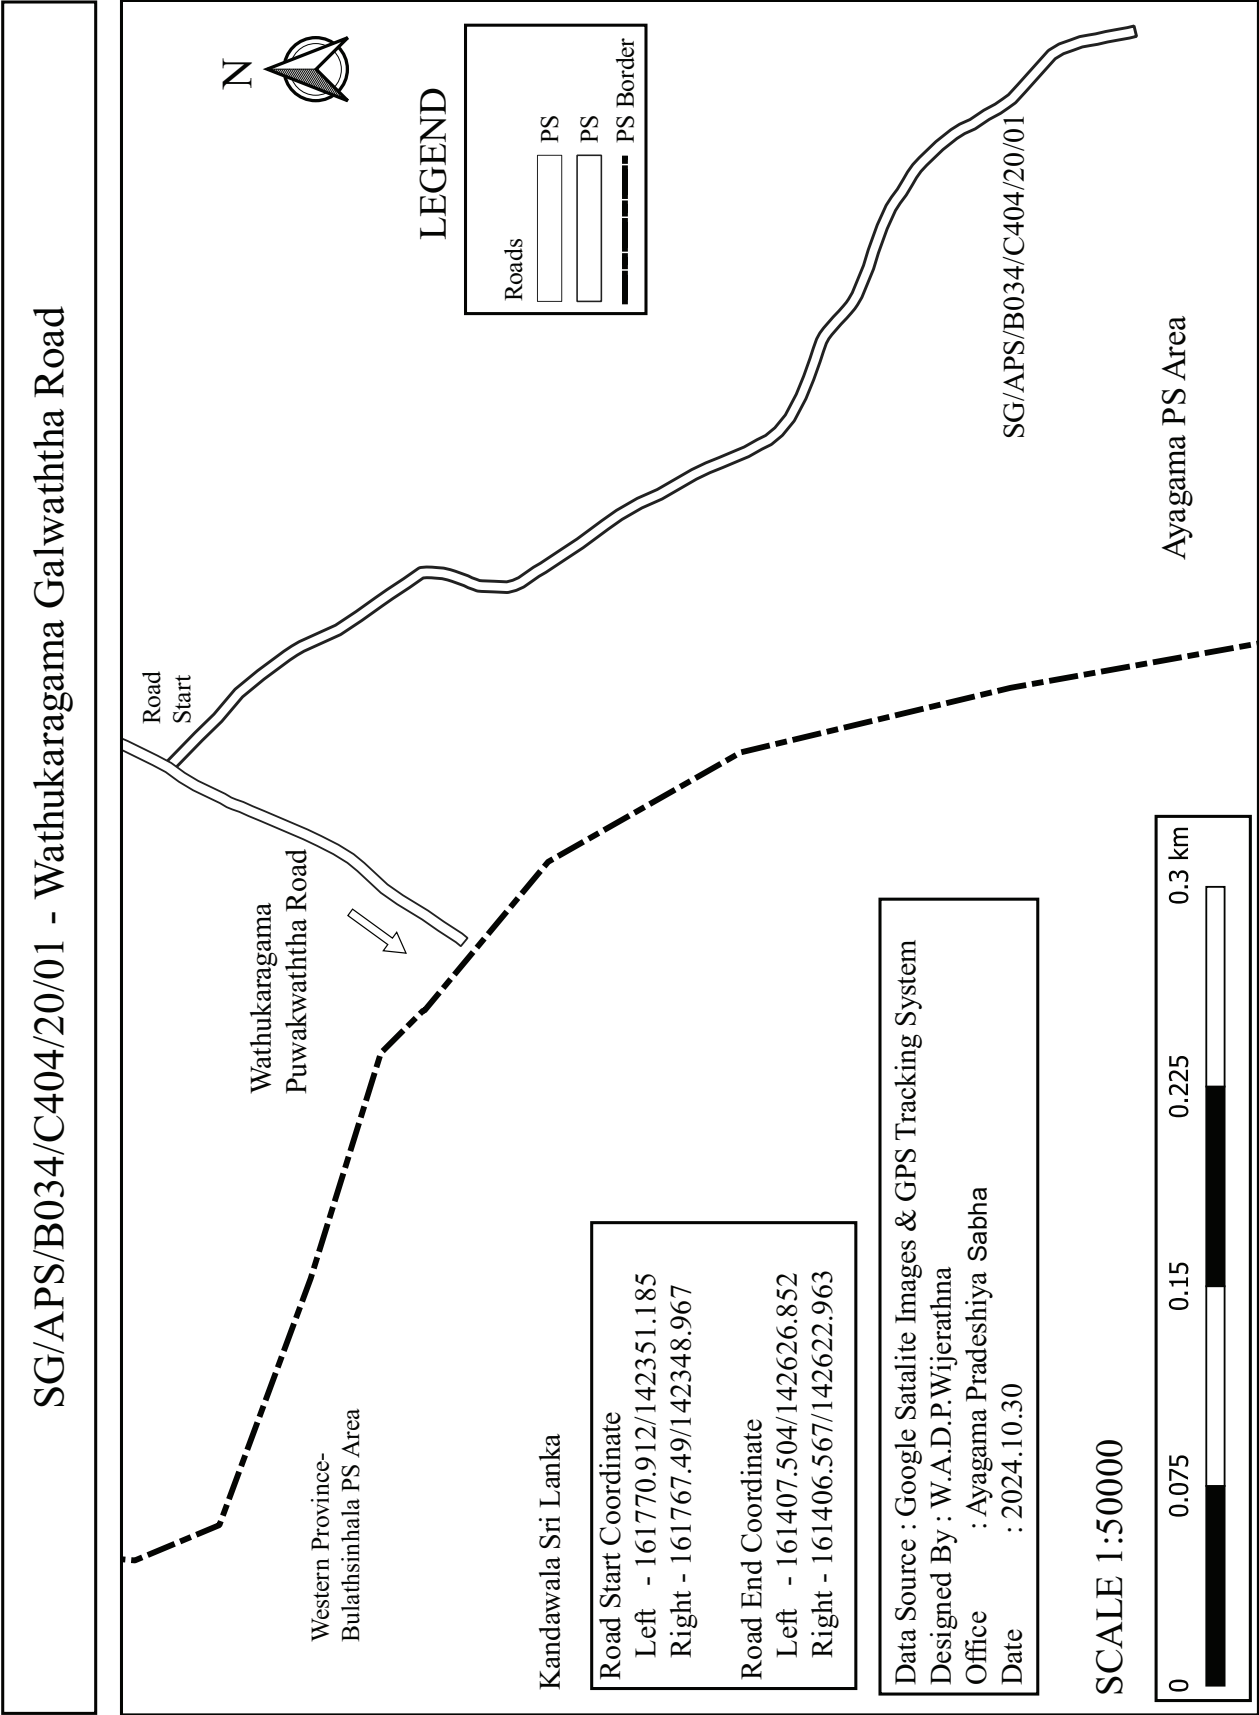


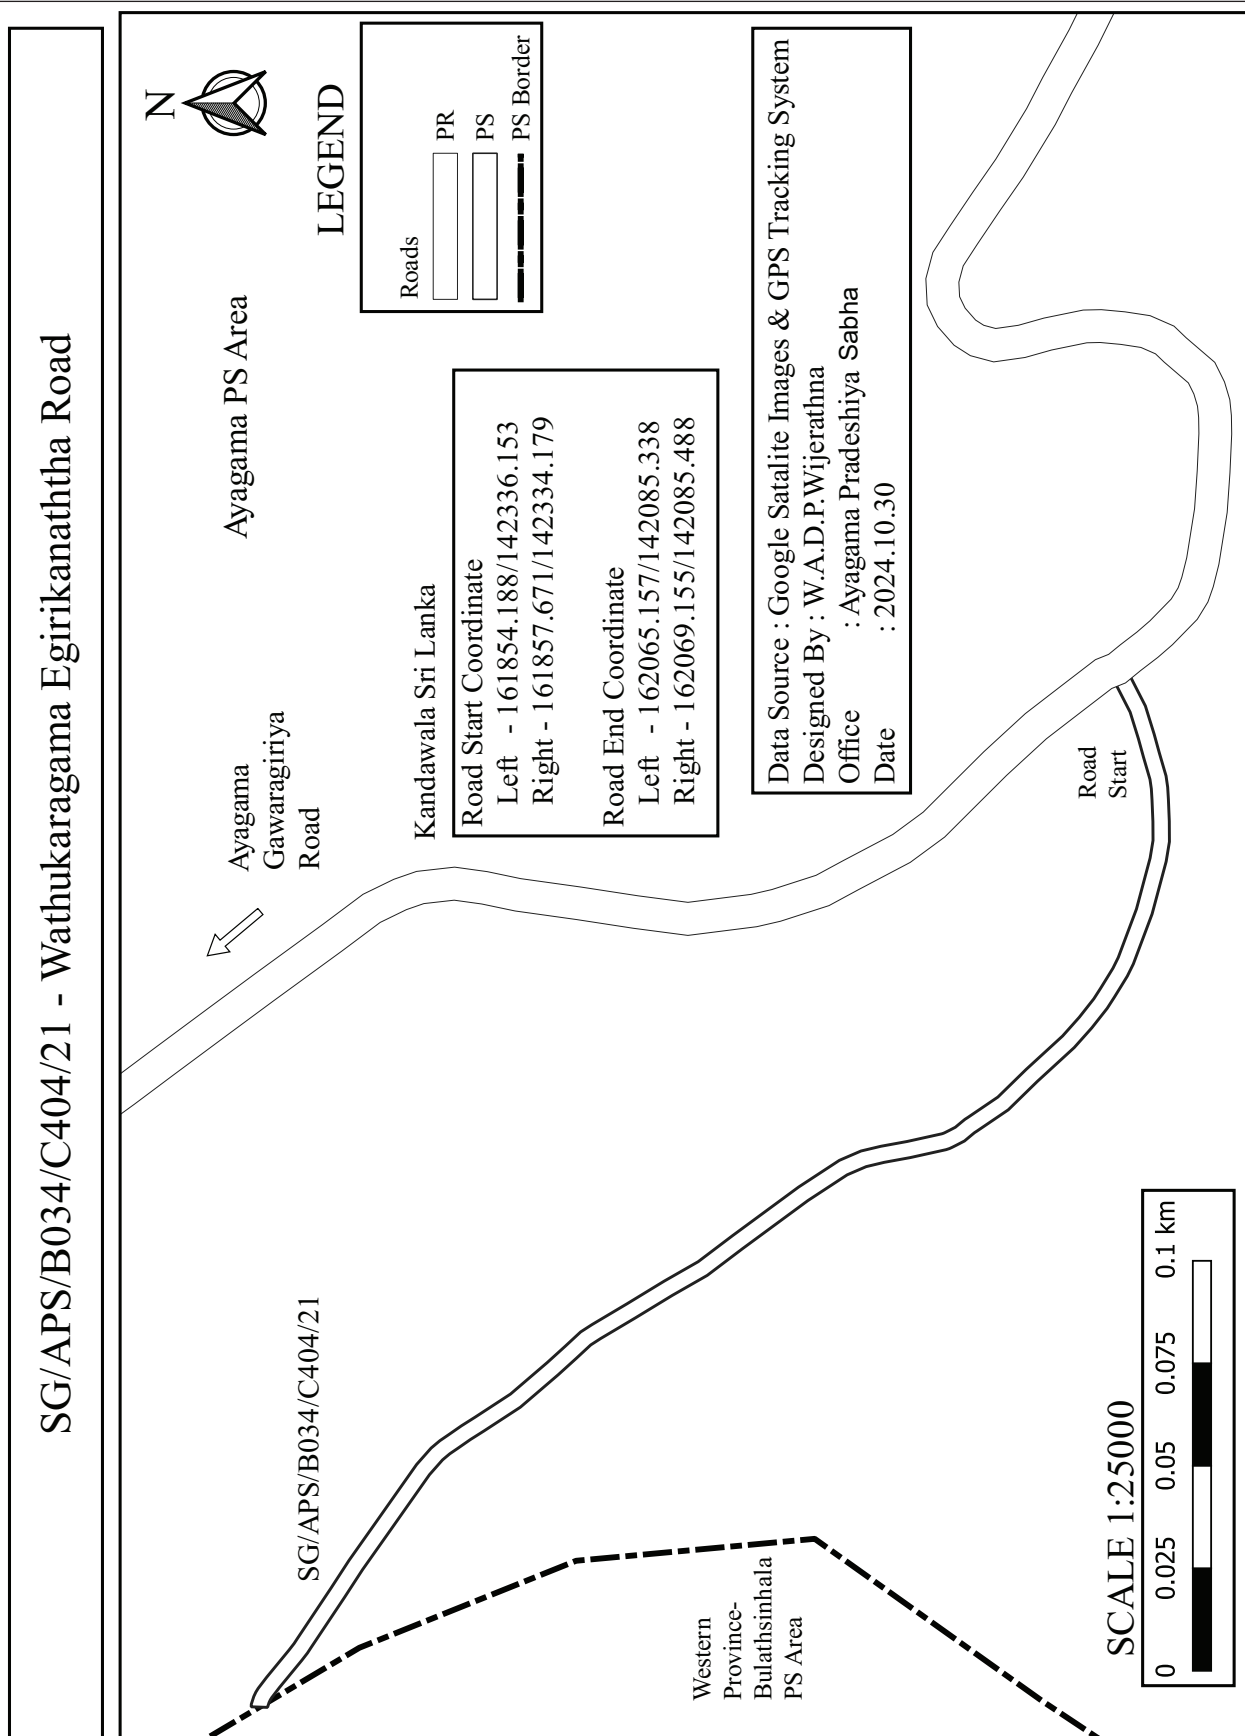


SG/APS/B034/C404/21/01 - First Lane of Wathukaragama Egirikanaththa Road

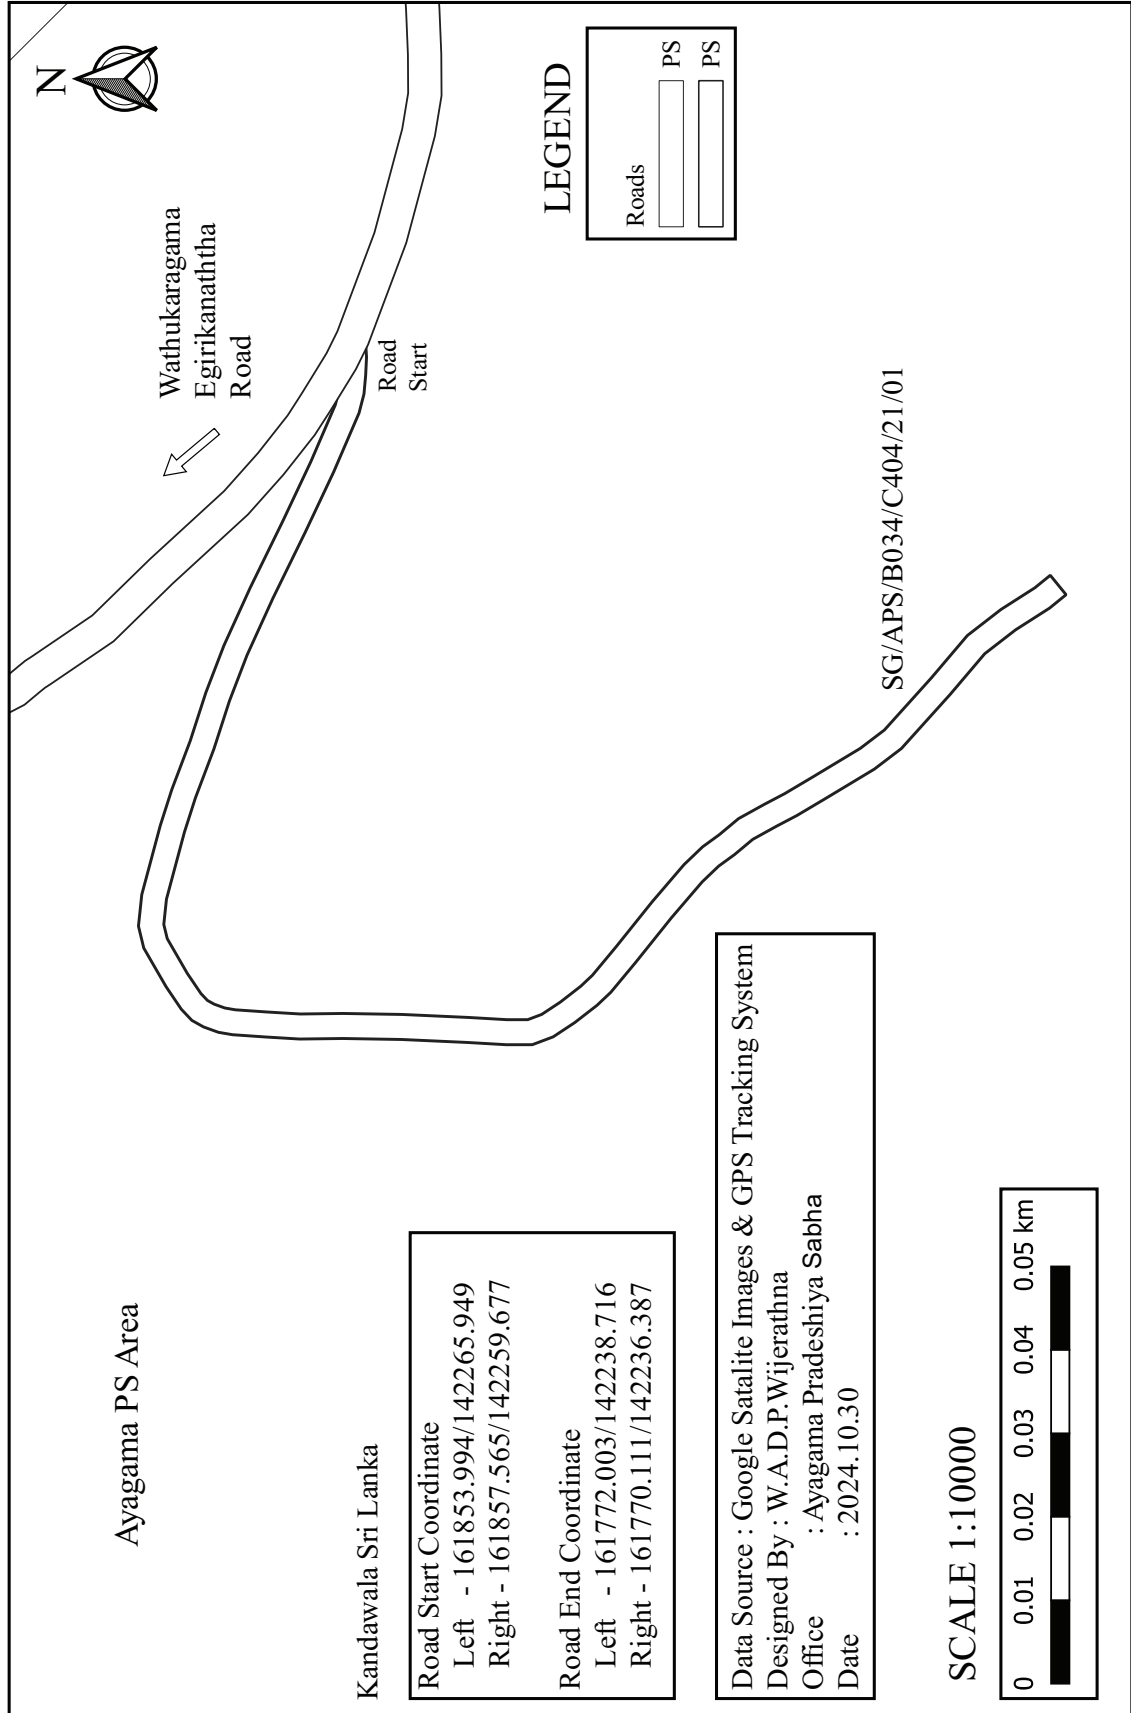


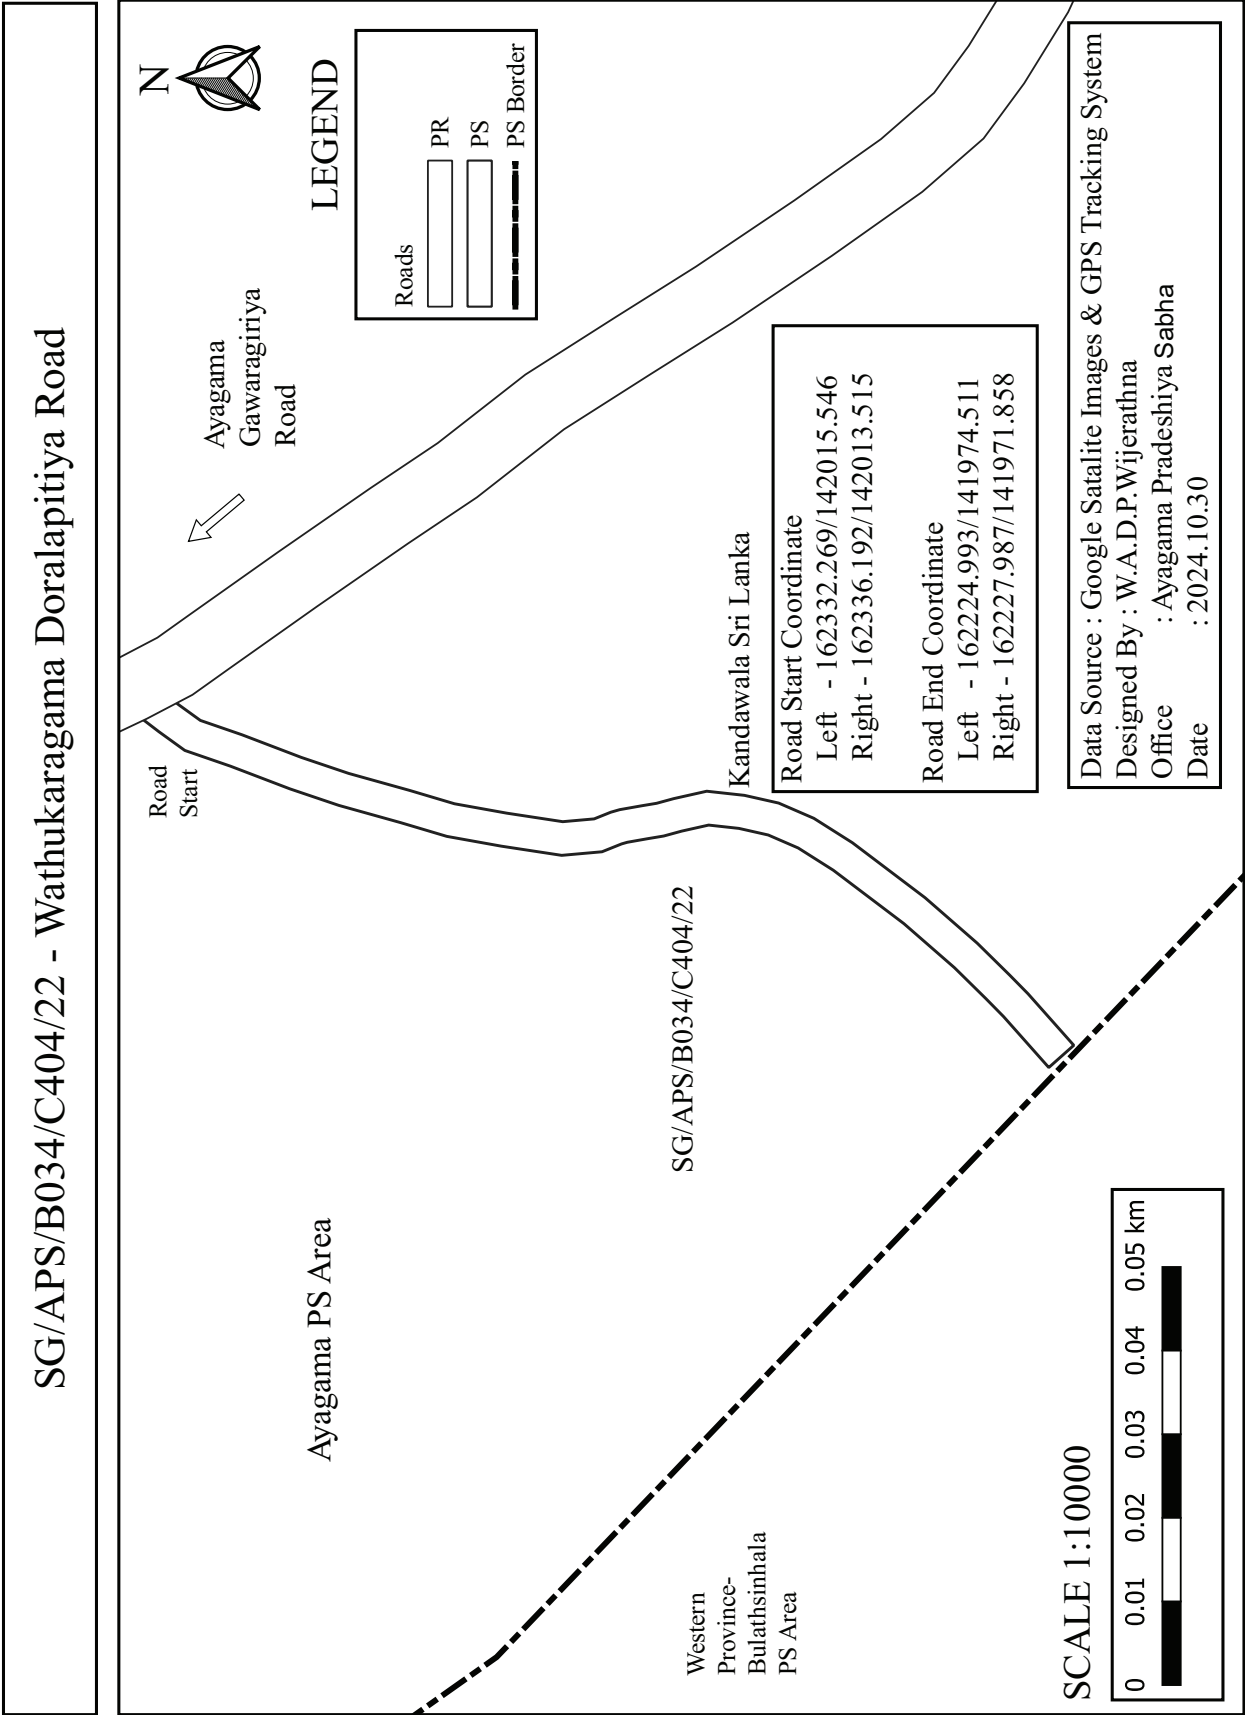


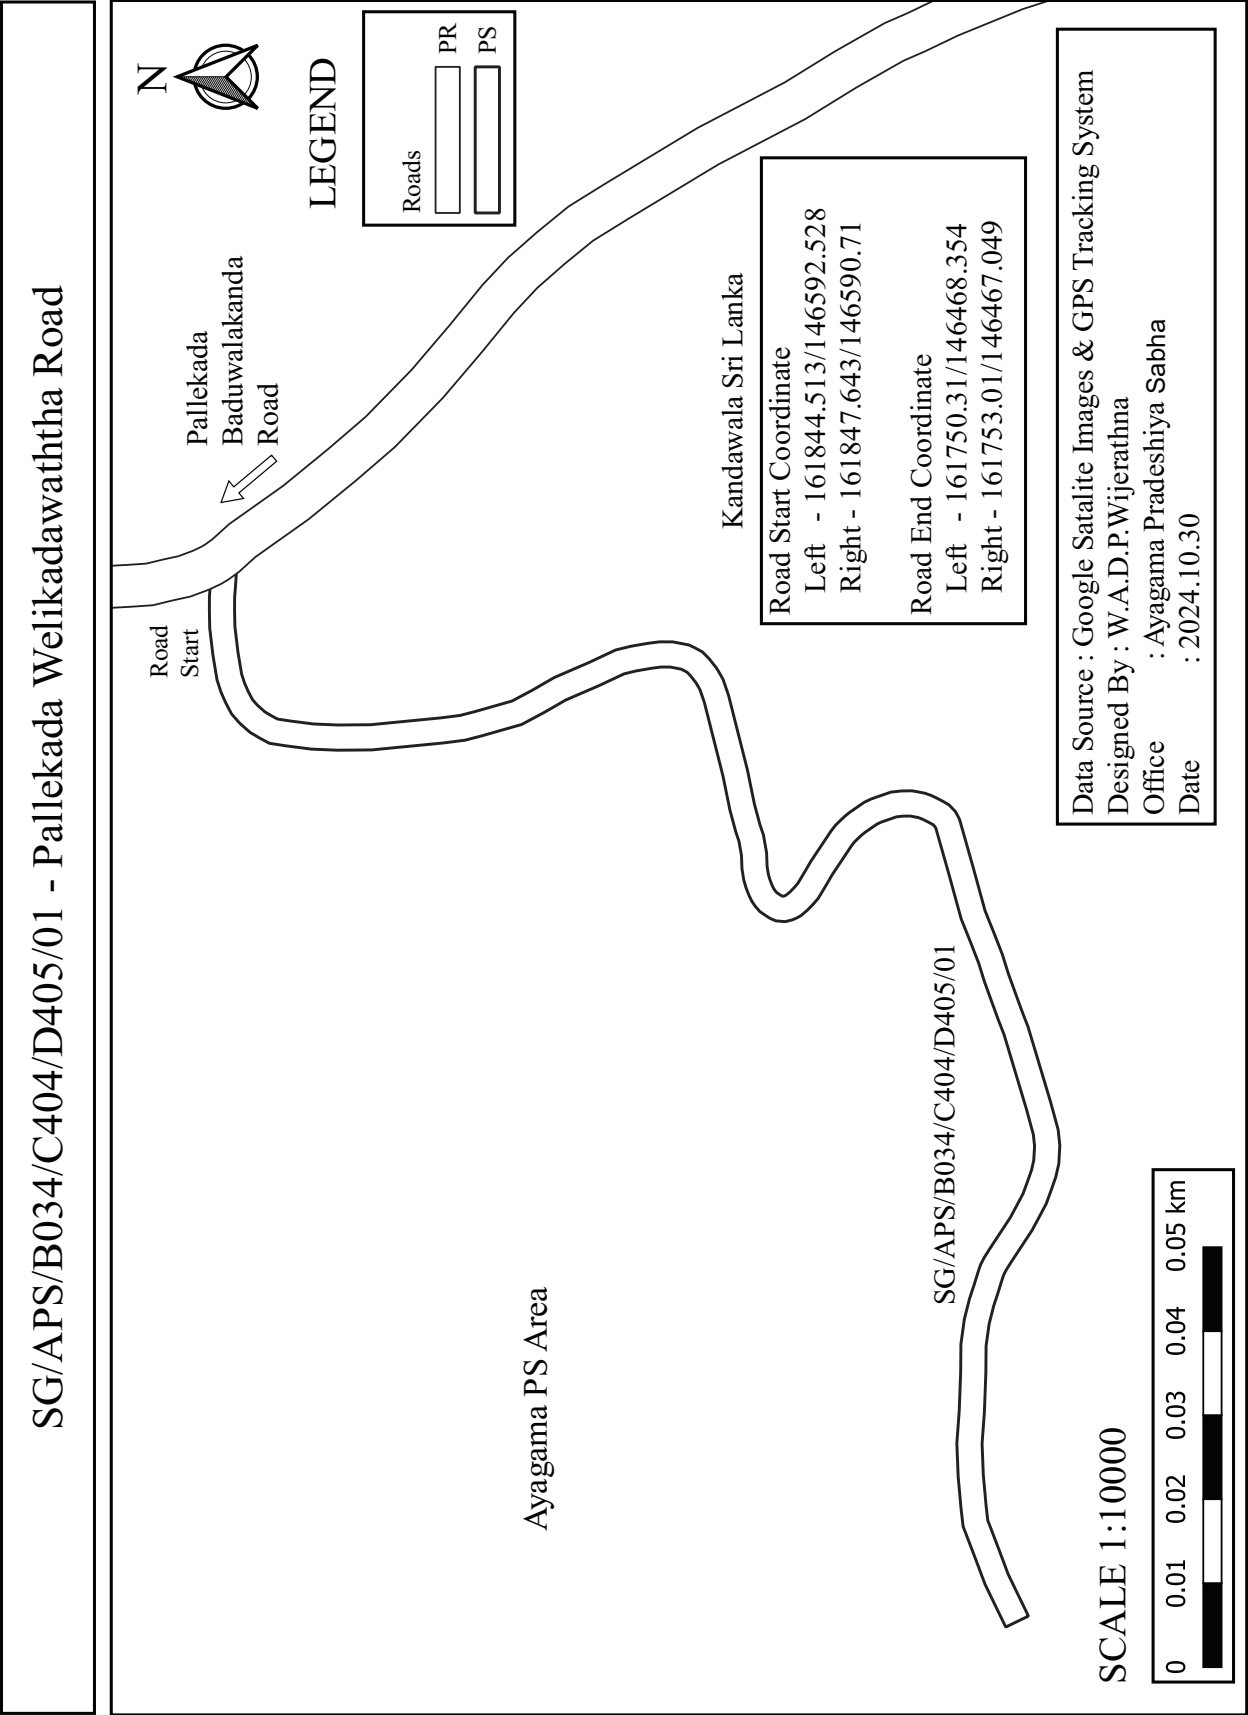

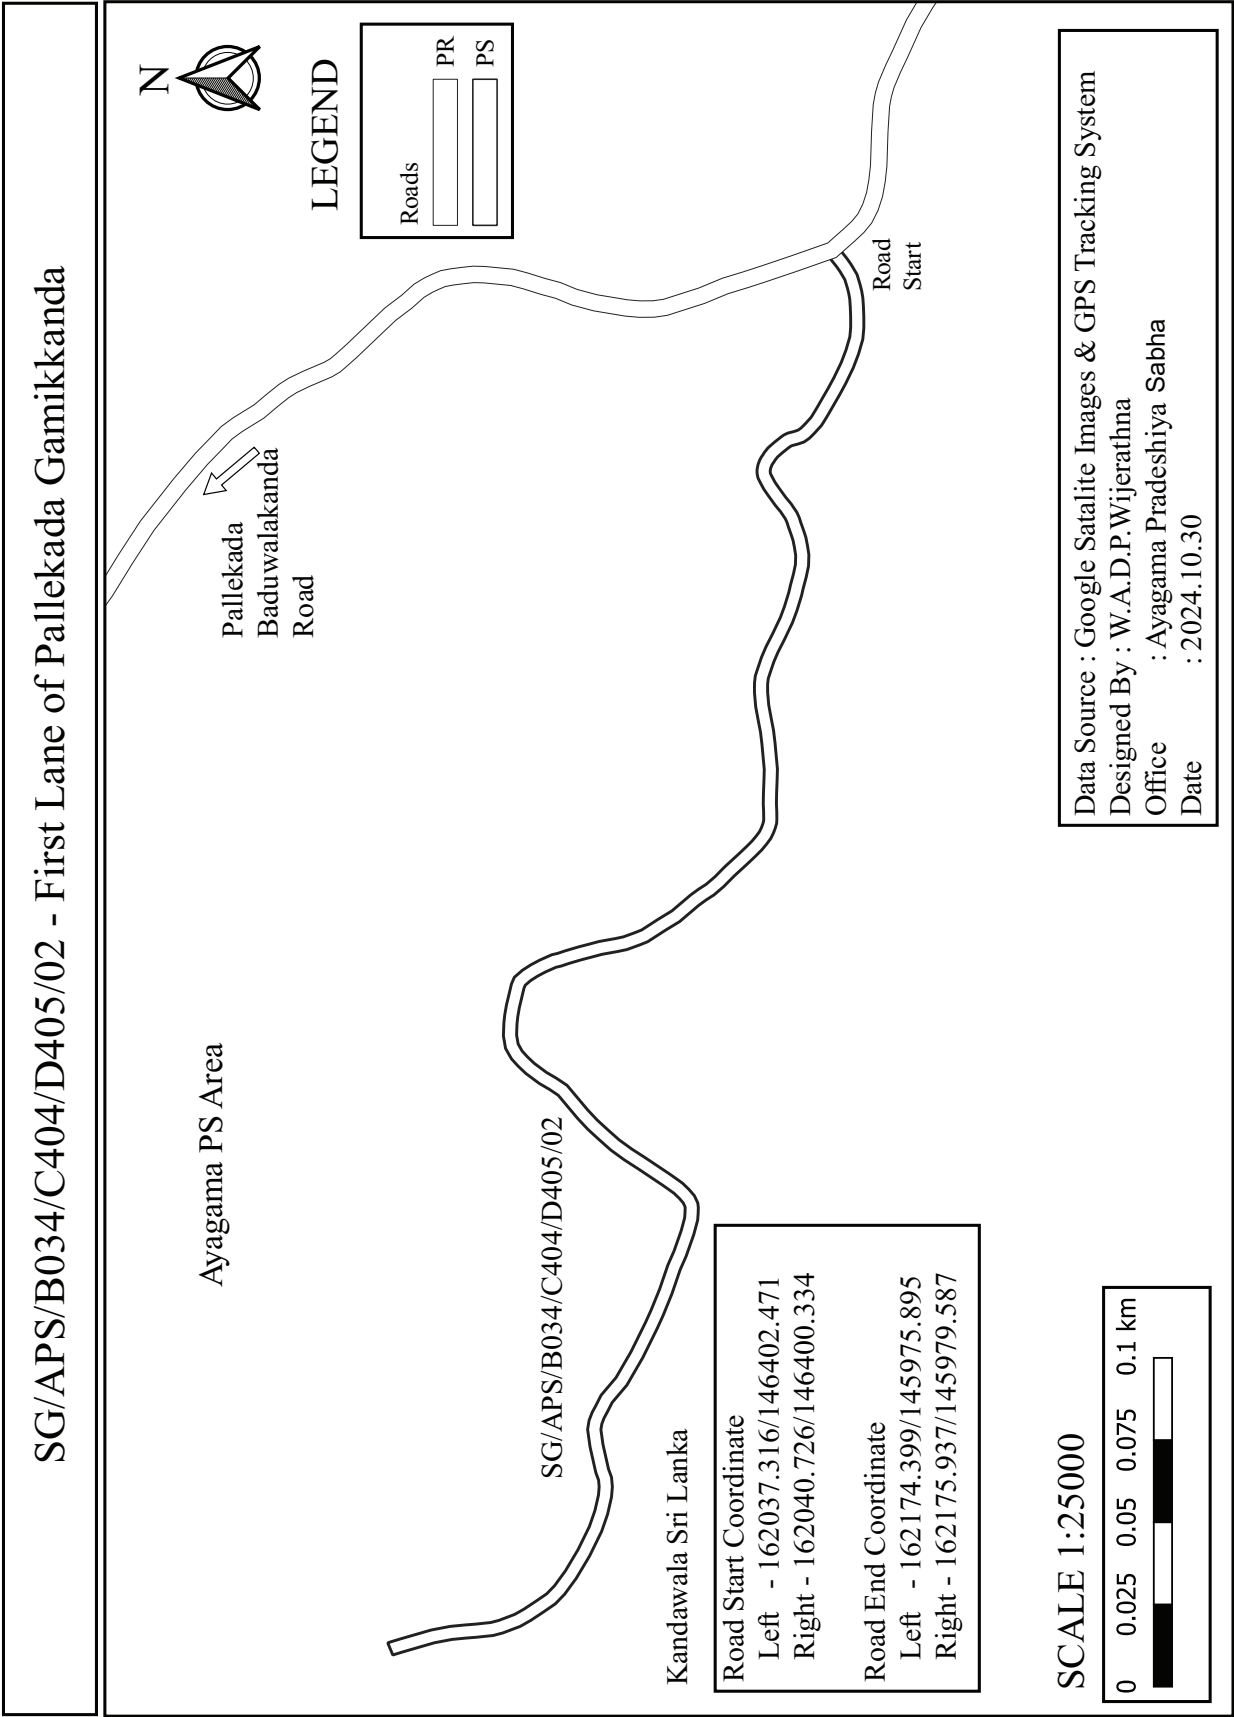



SG/APS/B034/C404/D405/03 - Second Lane of Pallekada Gamikkanda

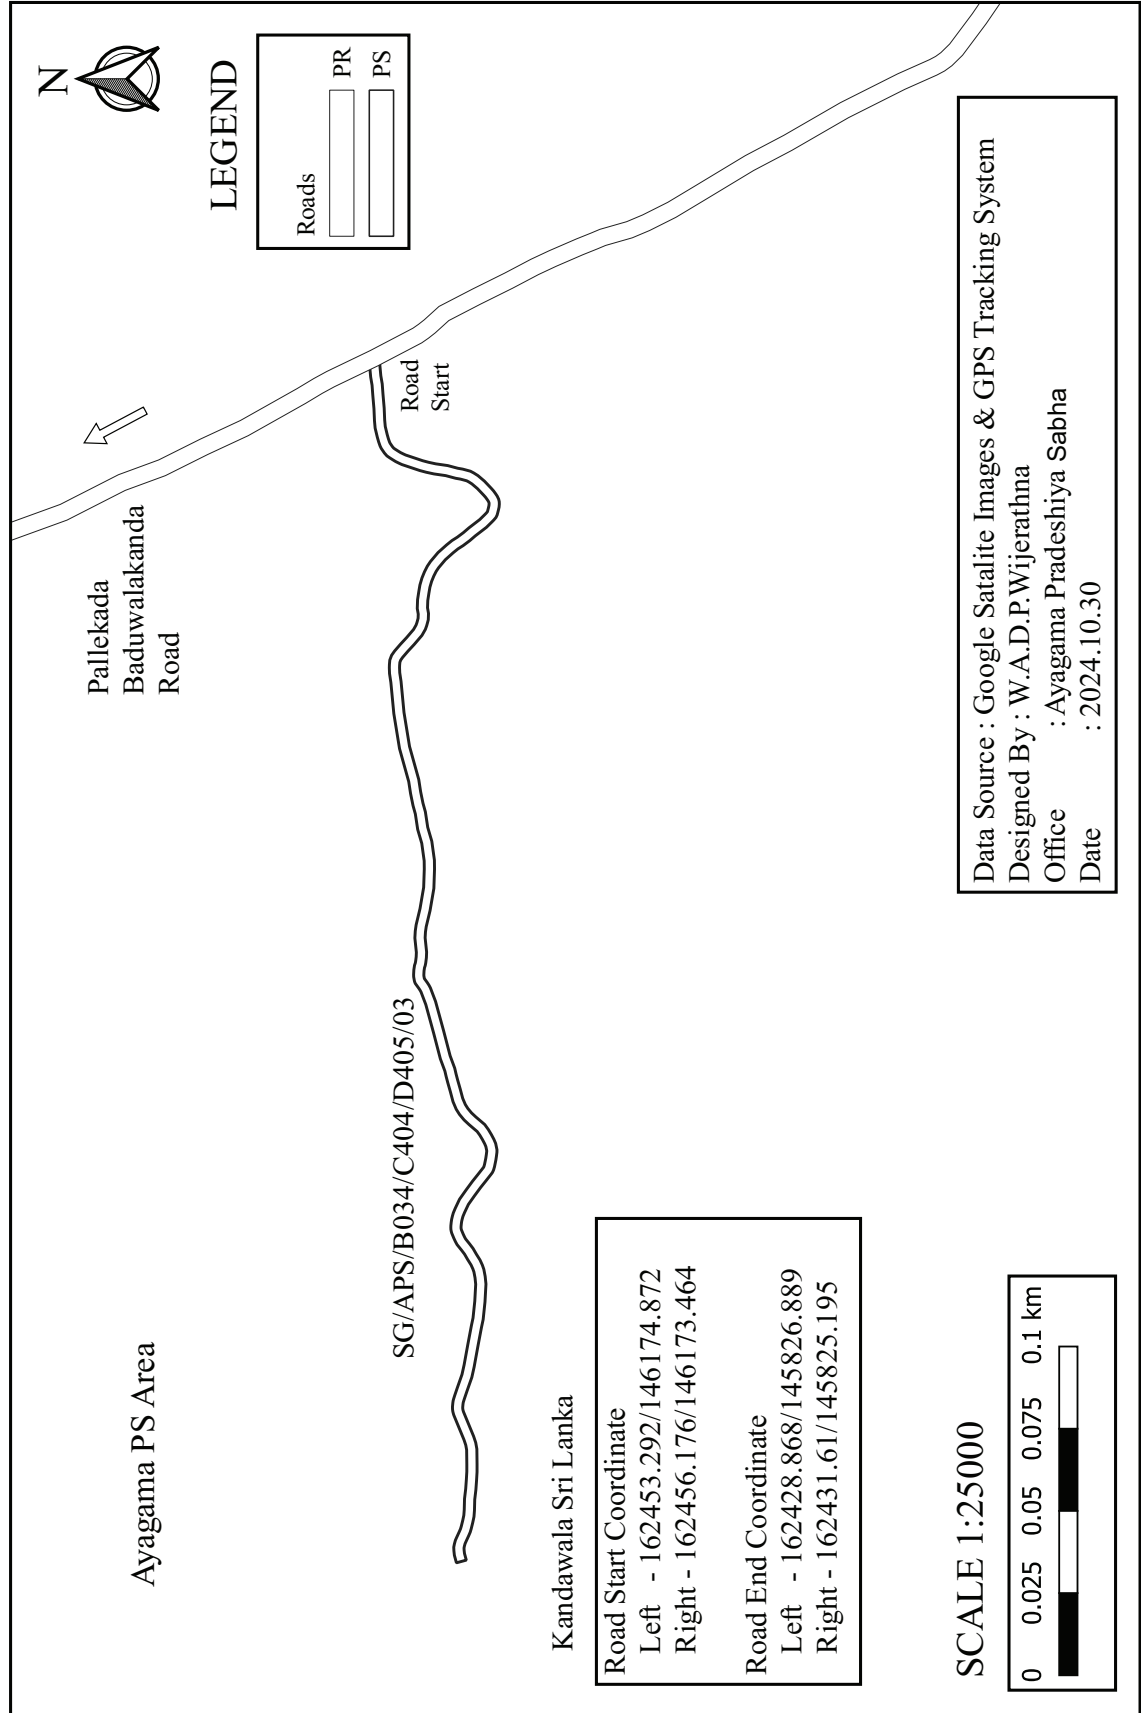


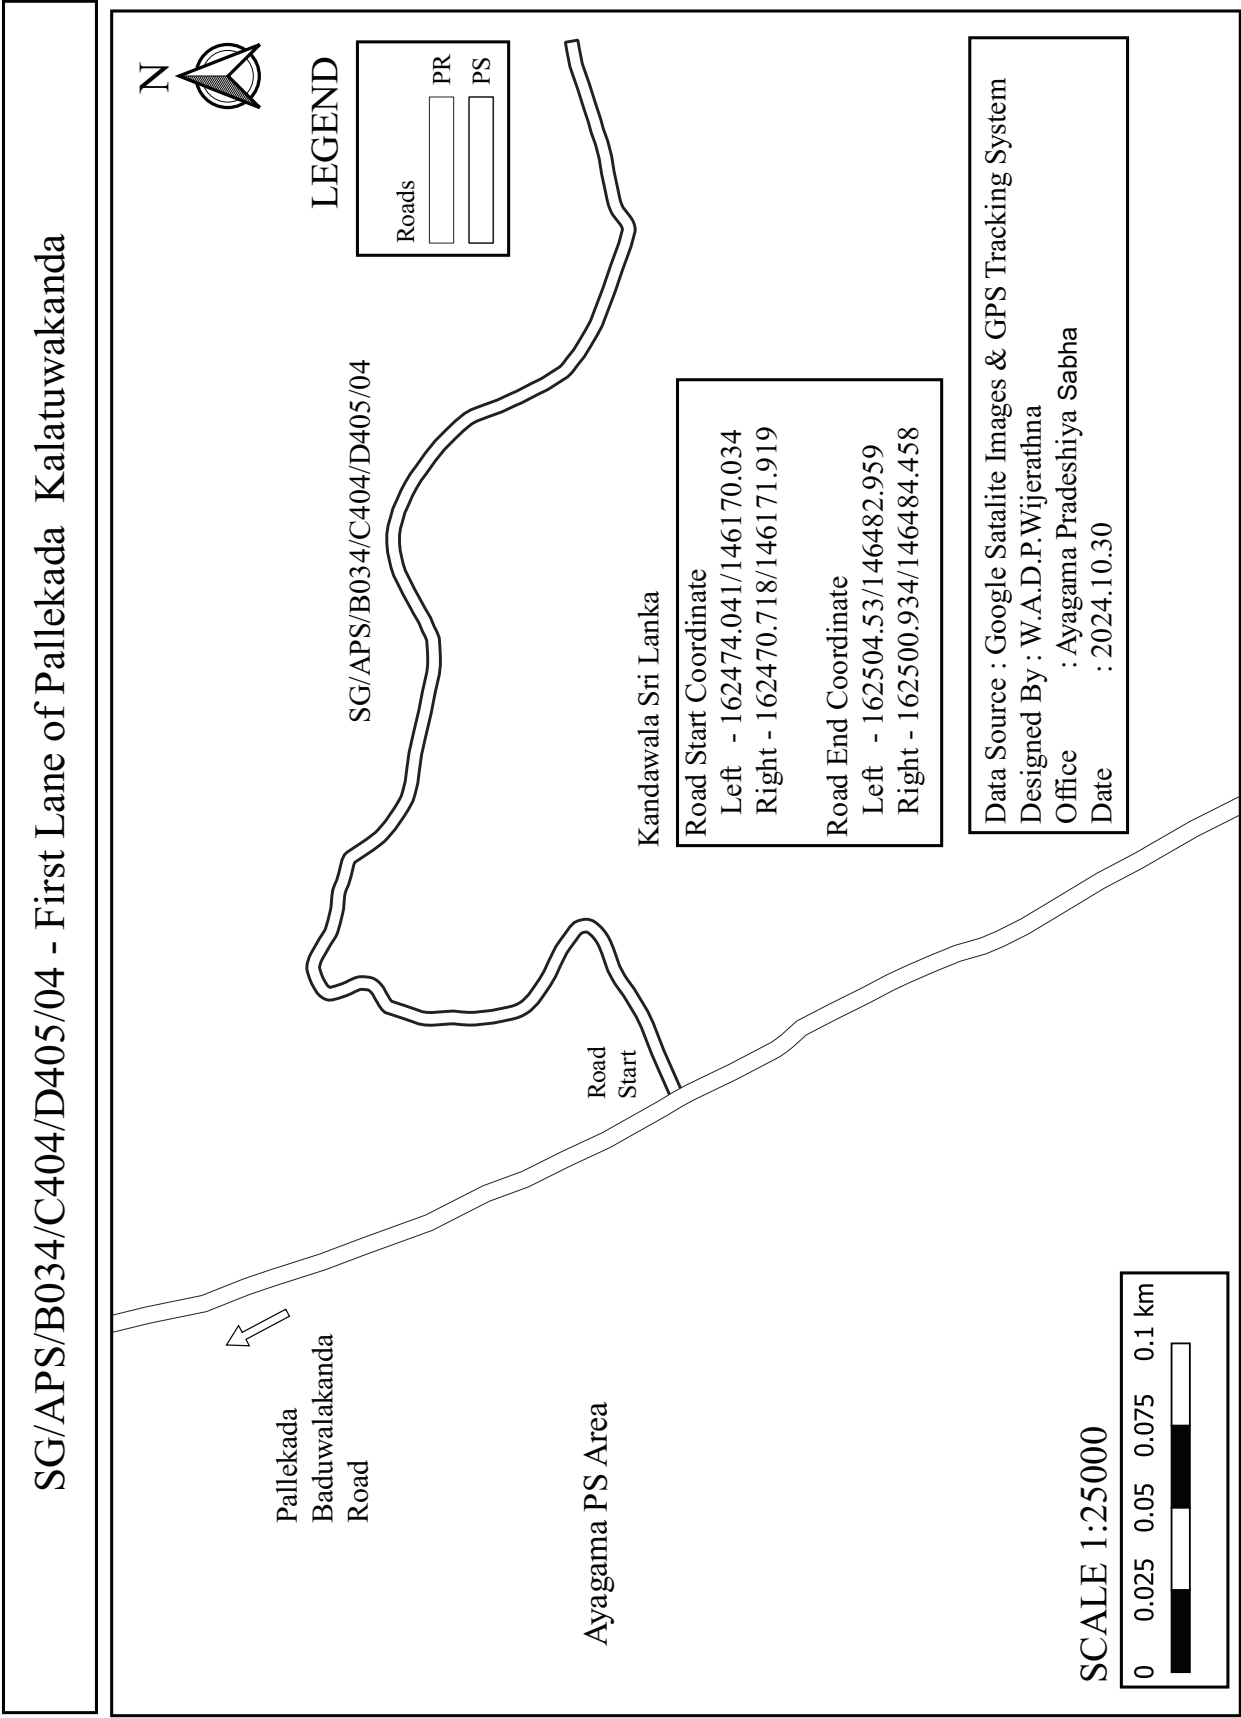



SG/APS/B034/C404/D405/05 - Second Lane Footpath of Pallekanda Kalatuwakanda

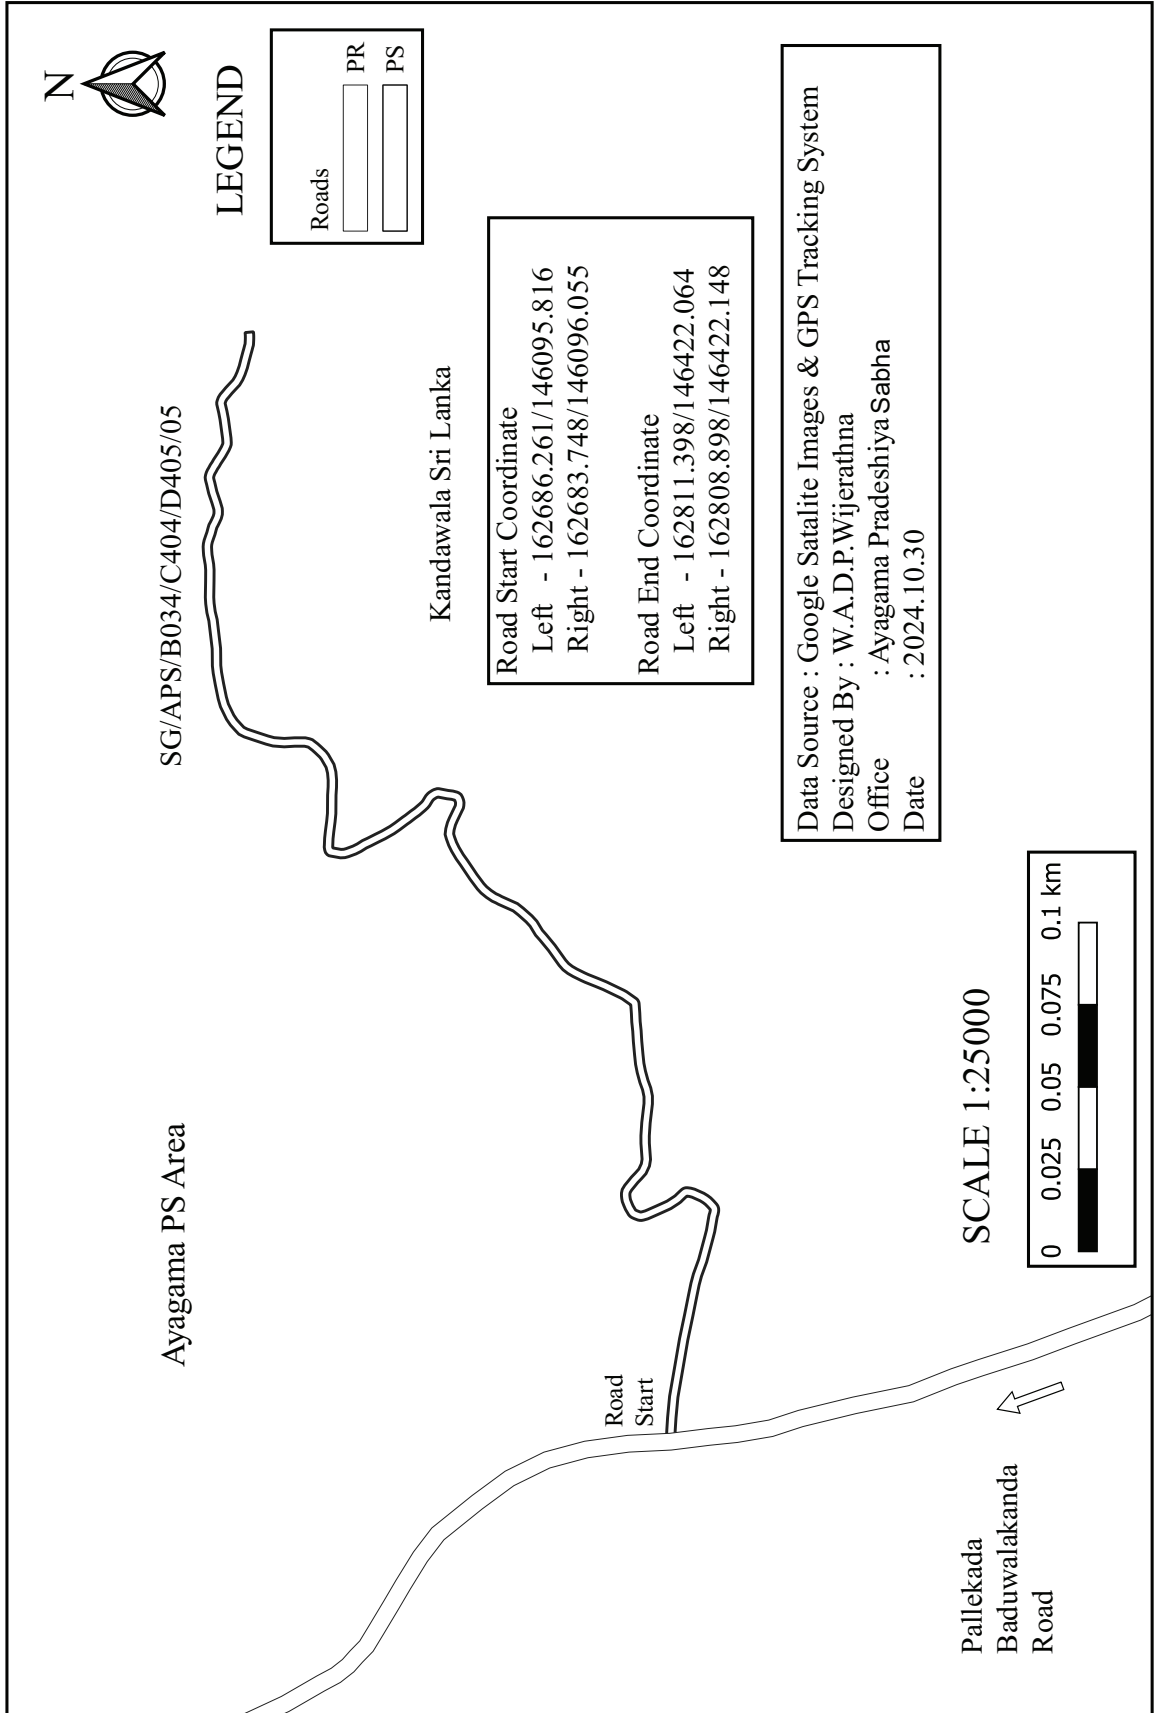


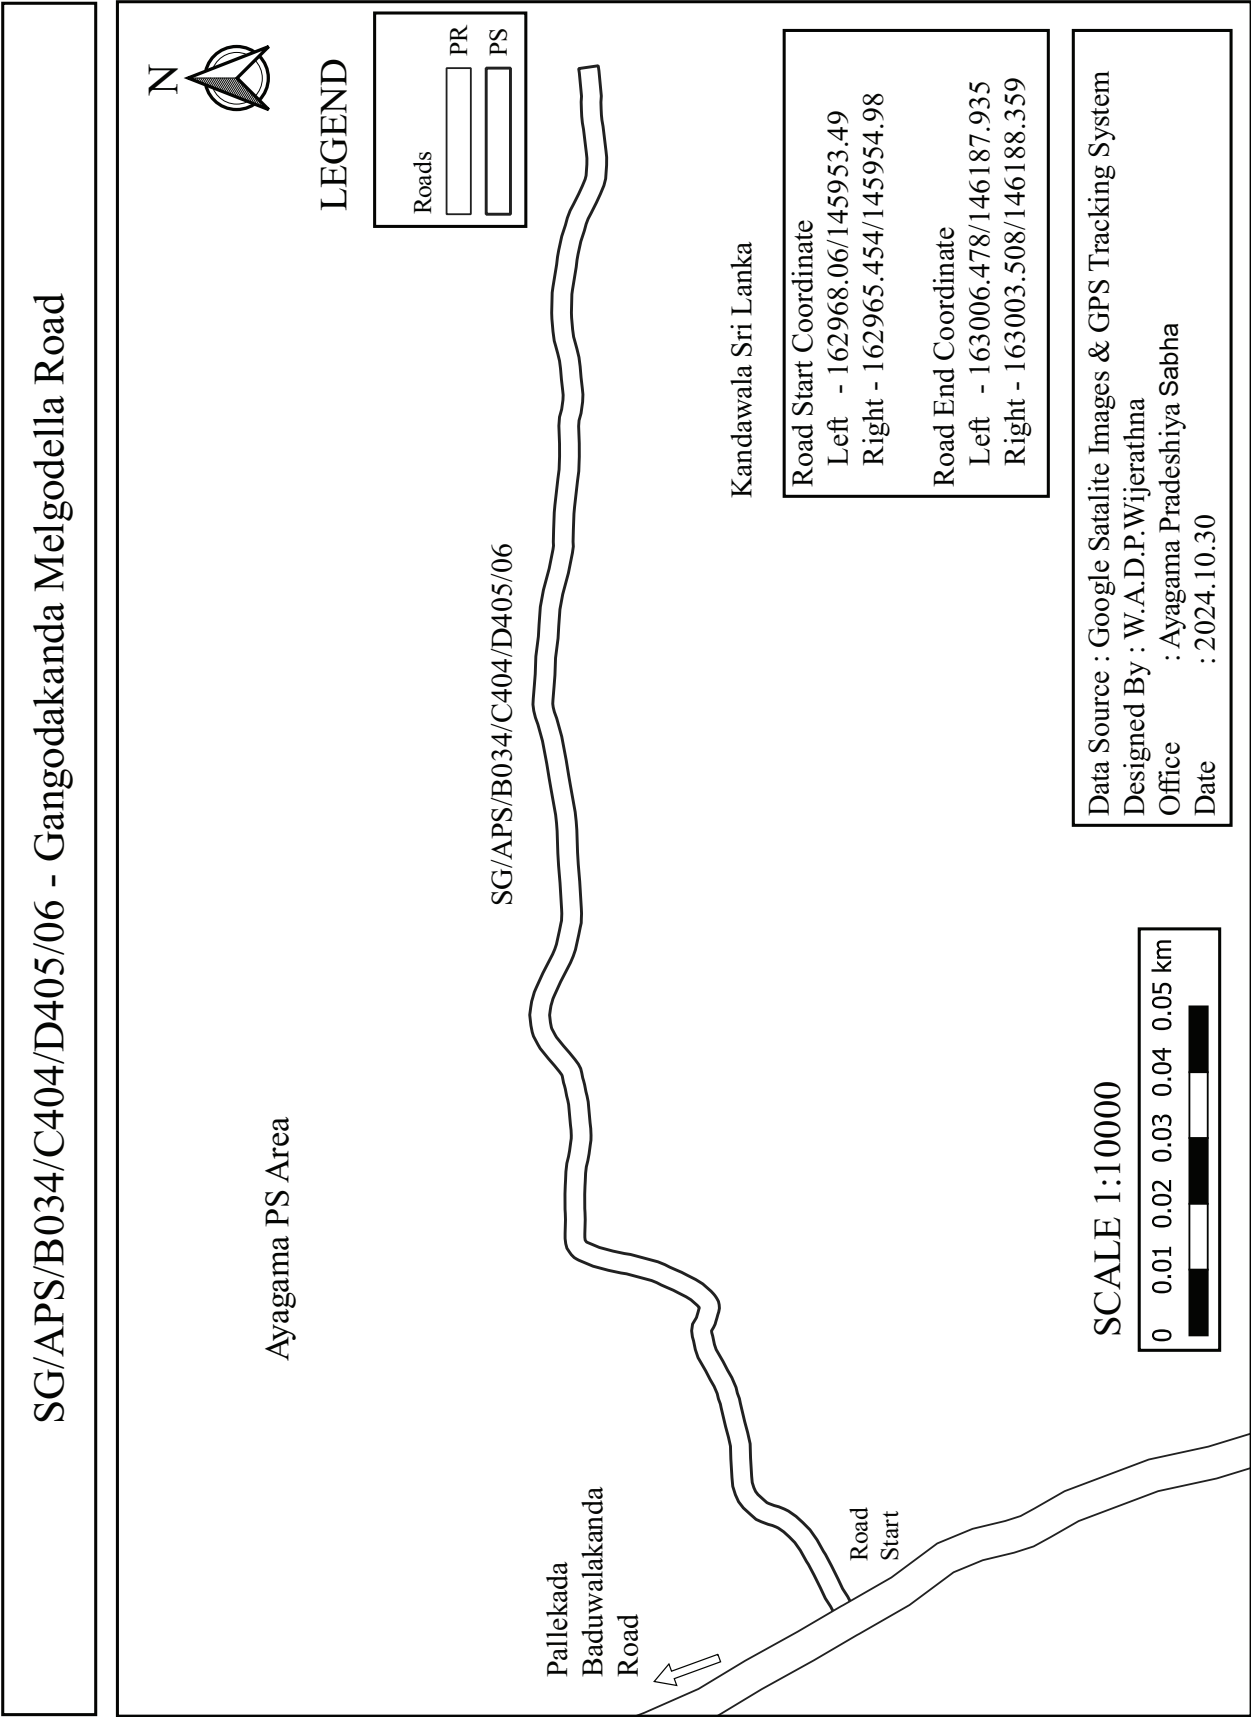


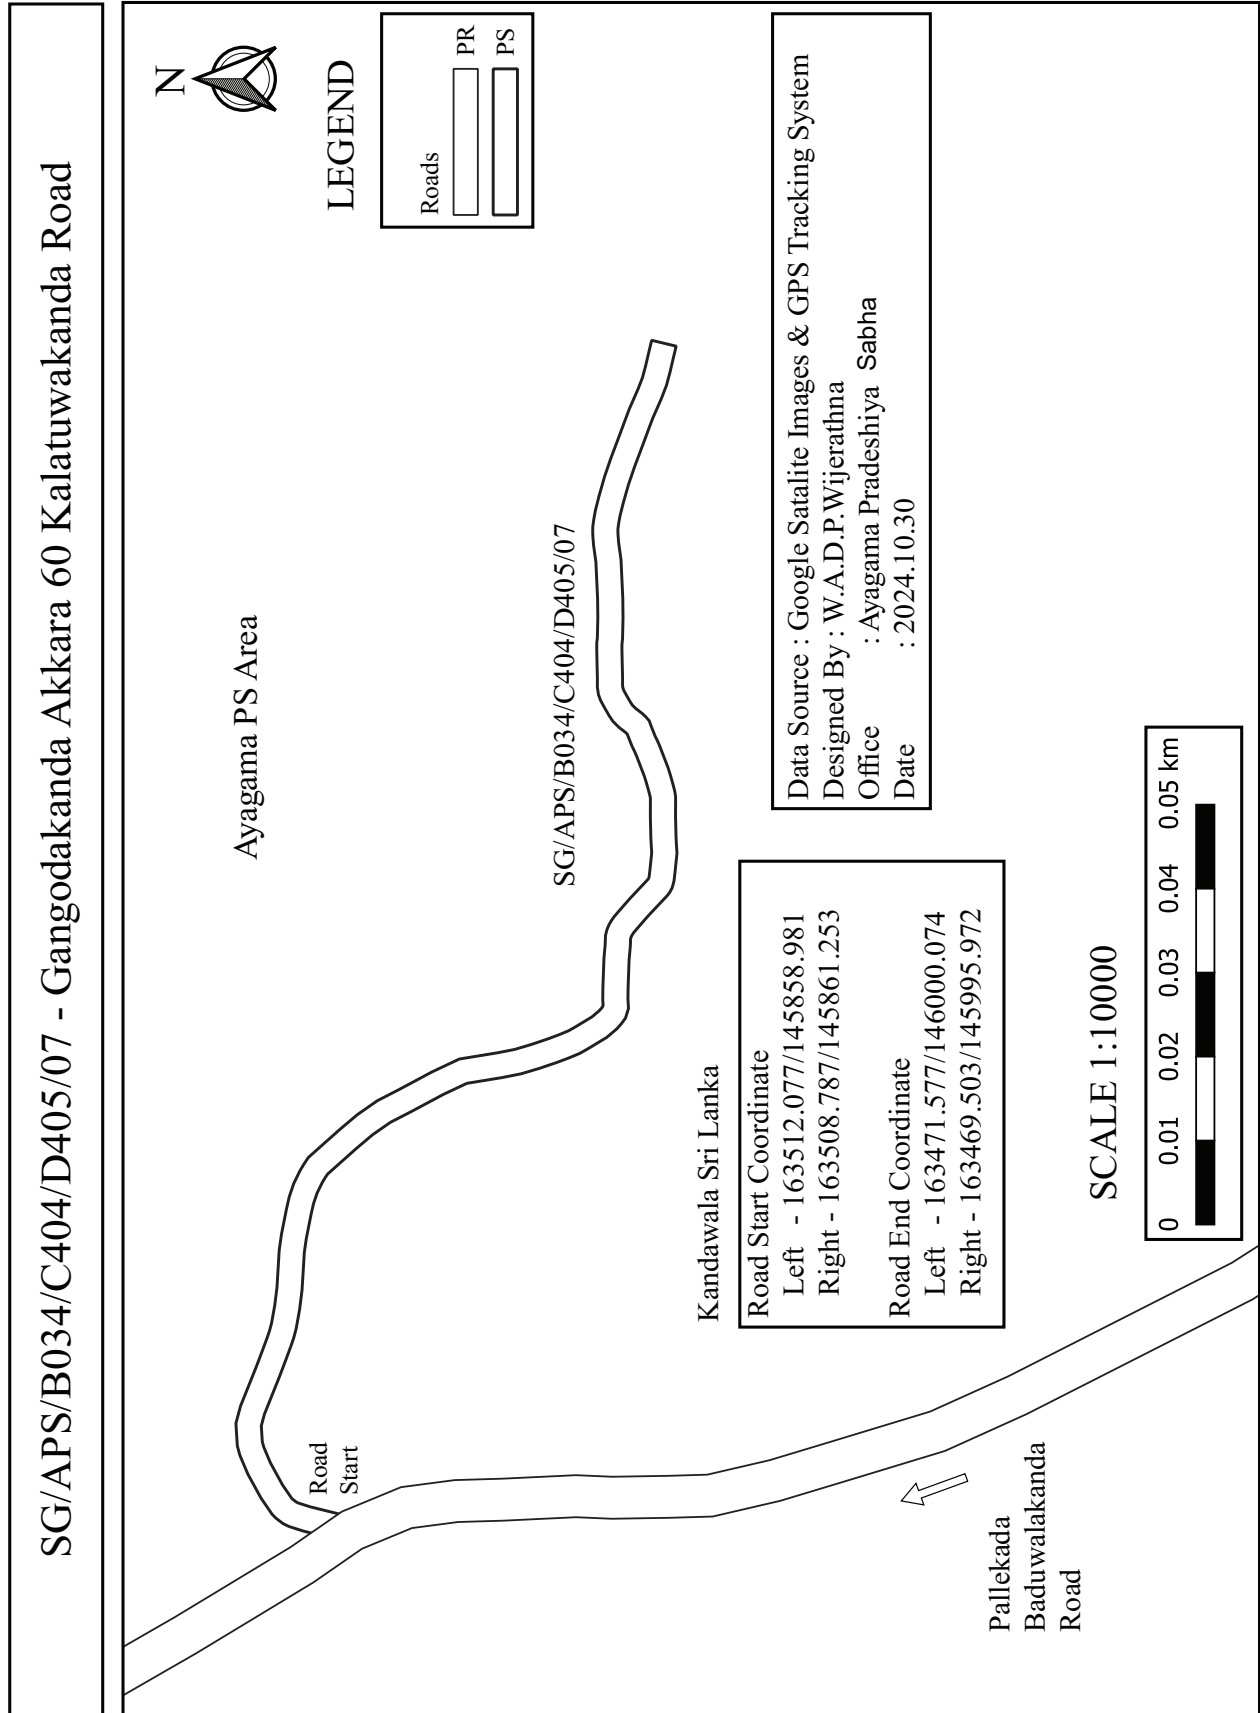


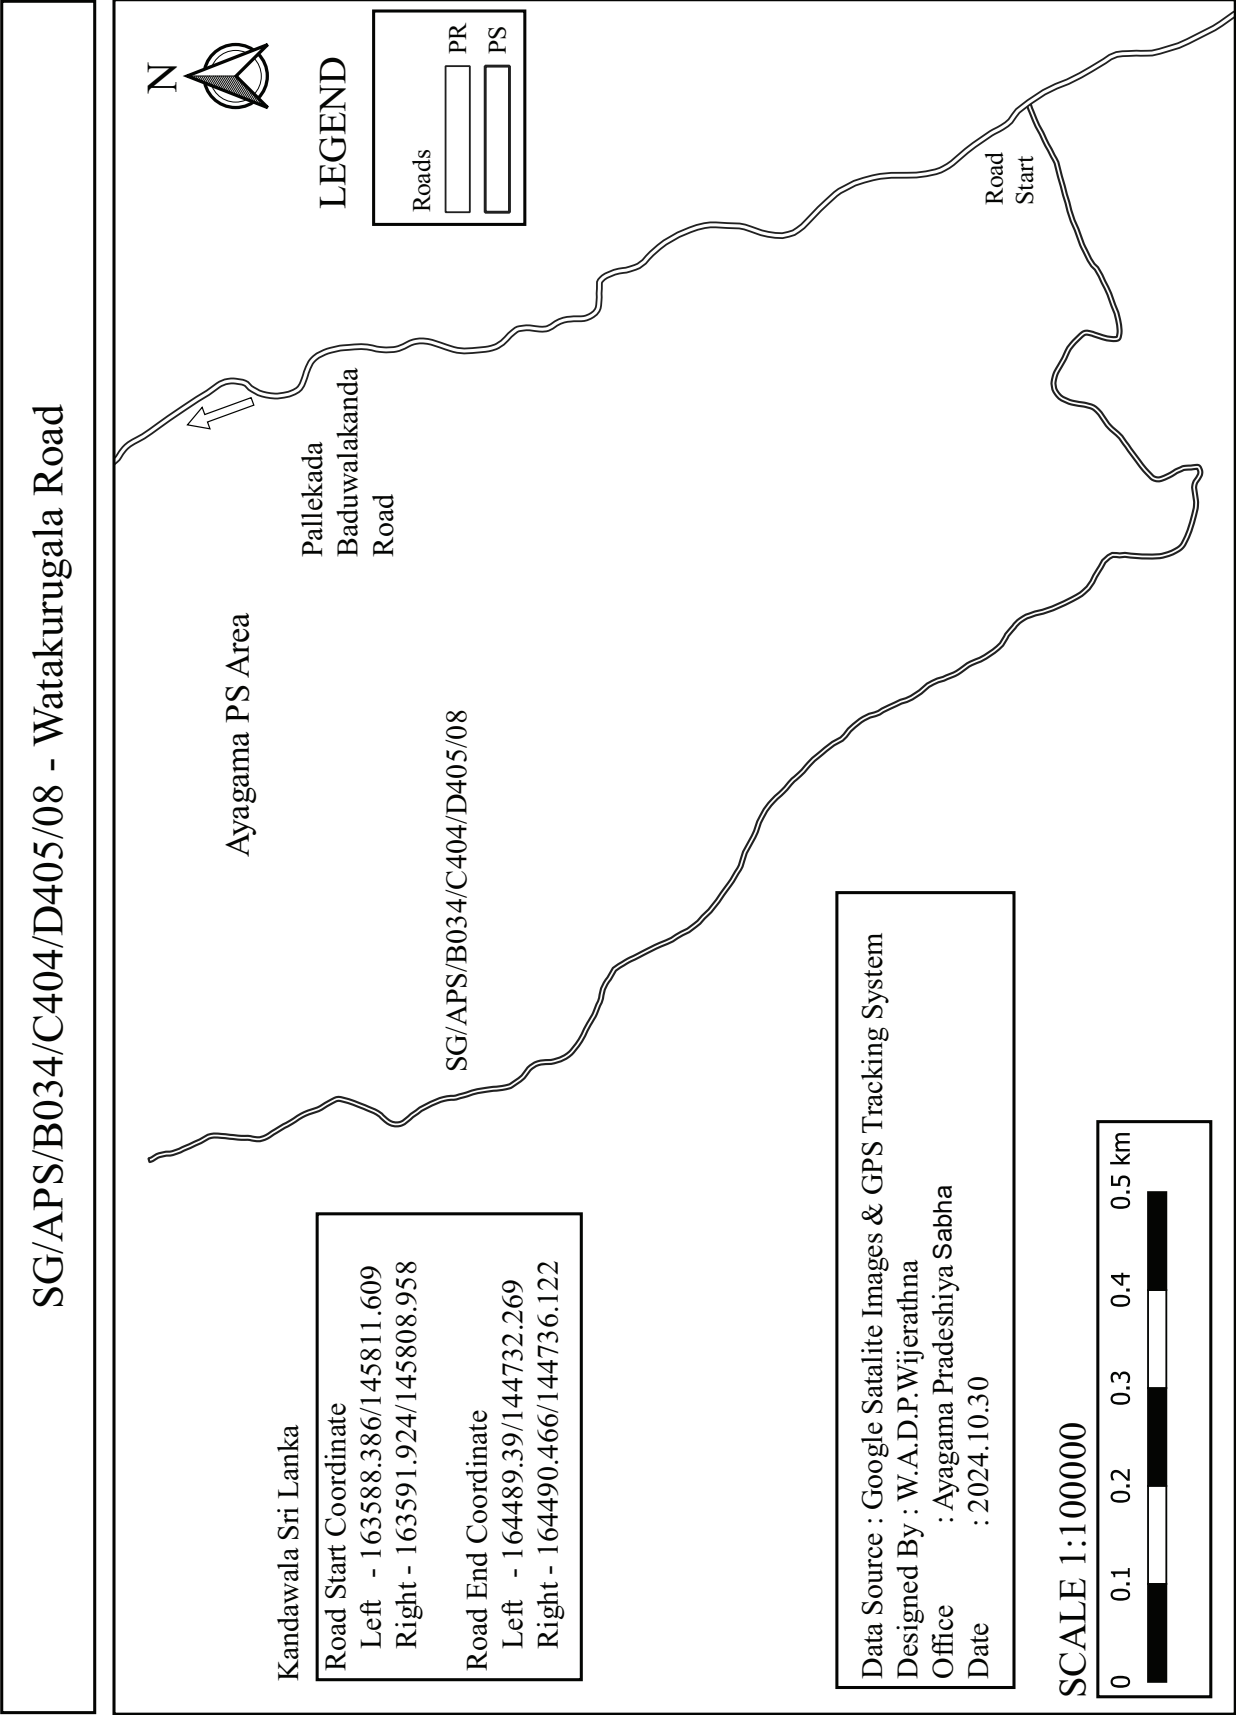


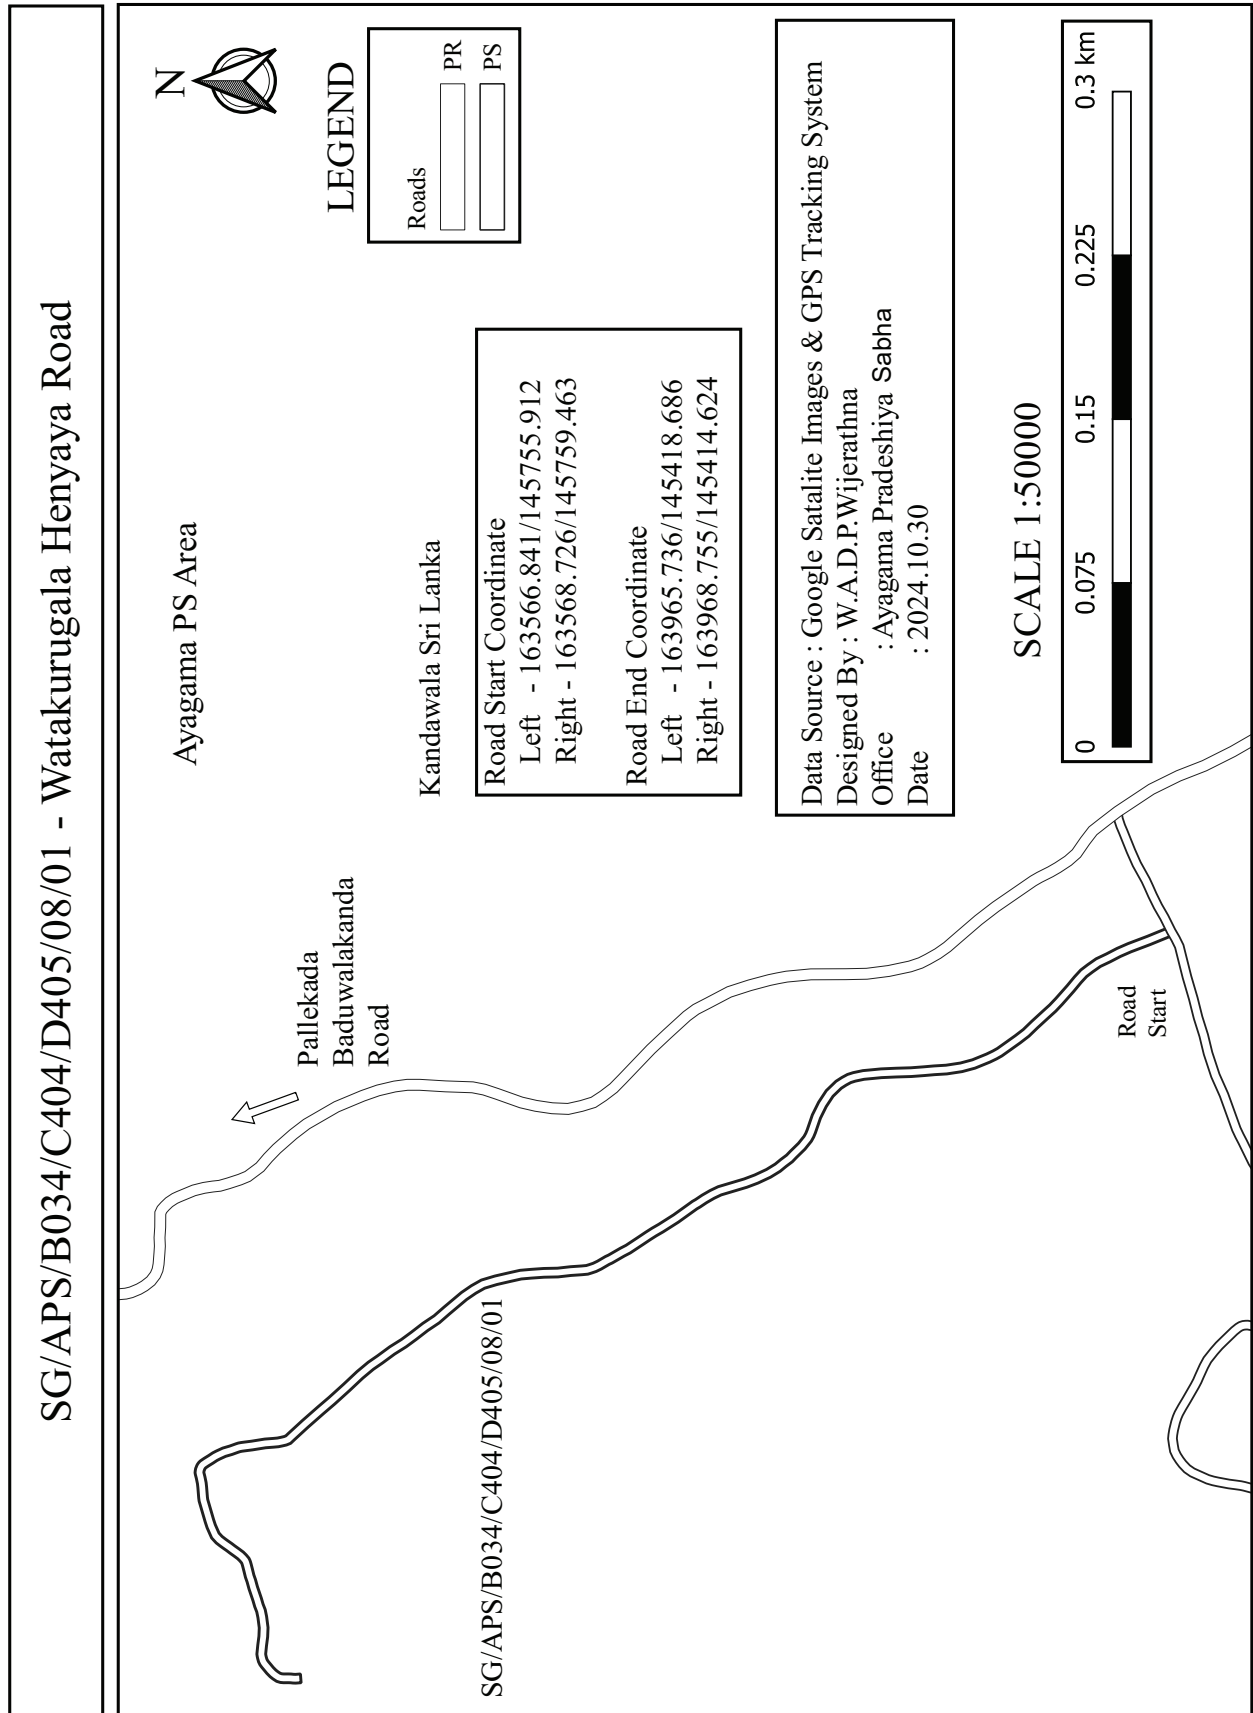


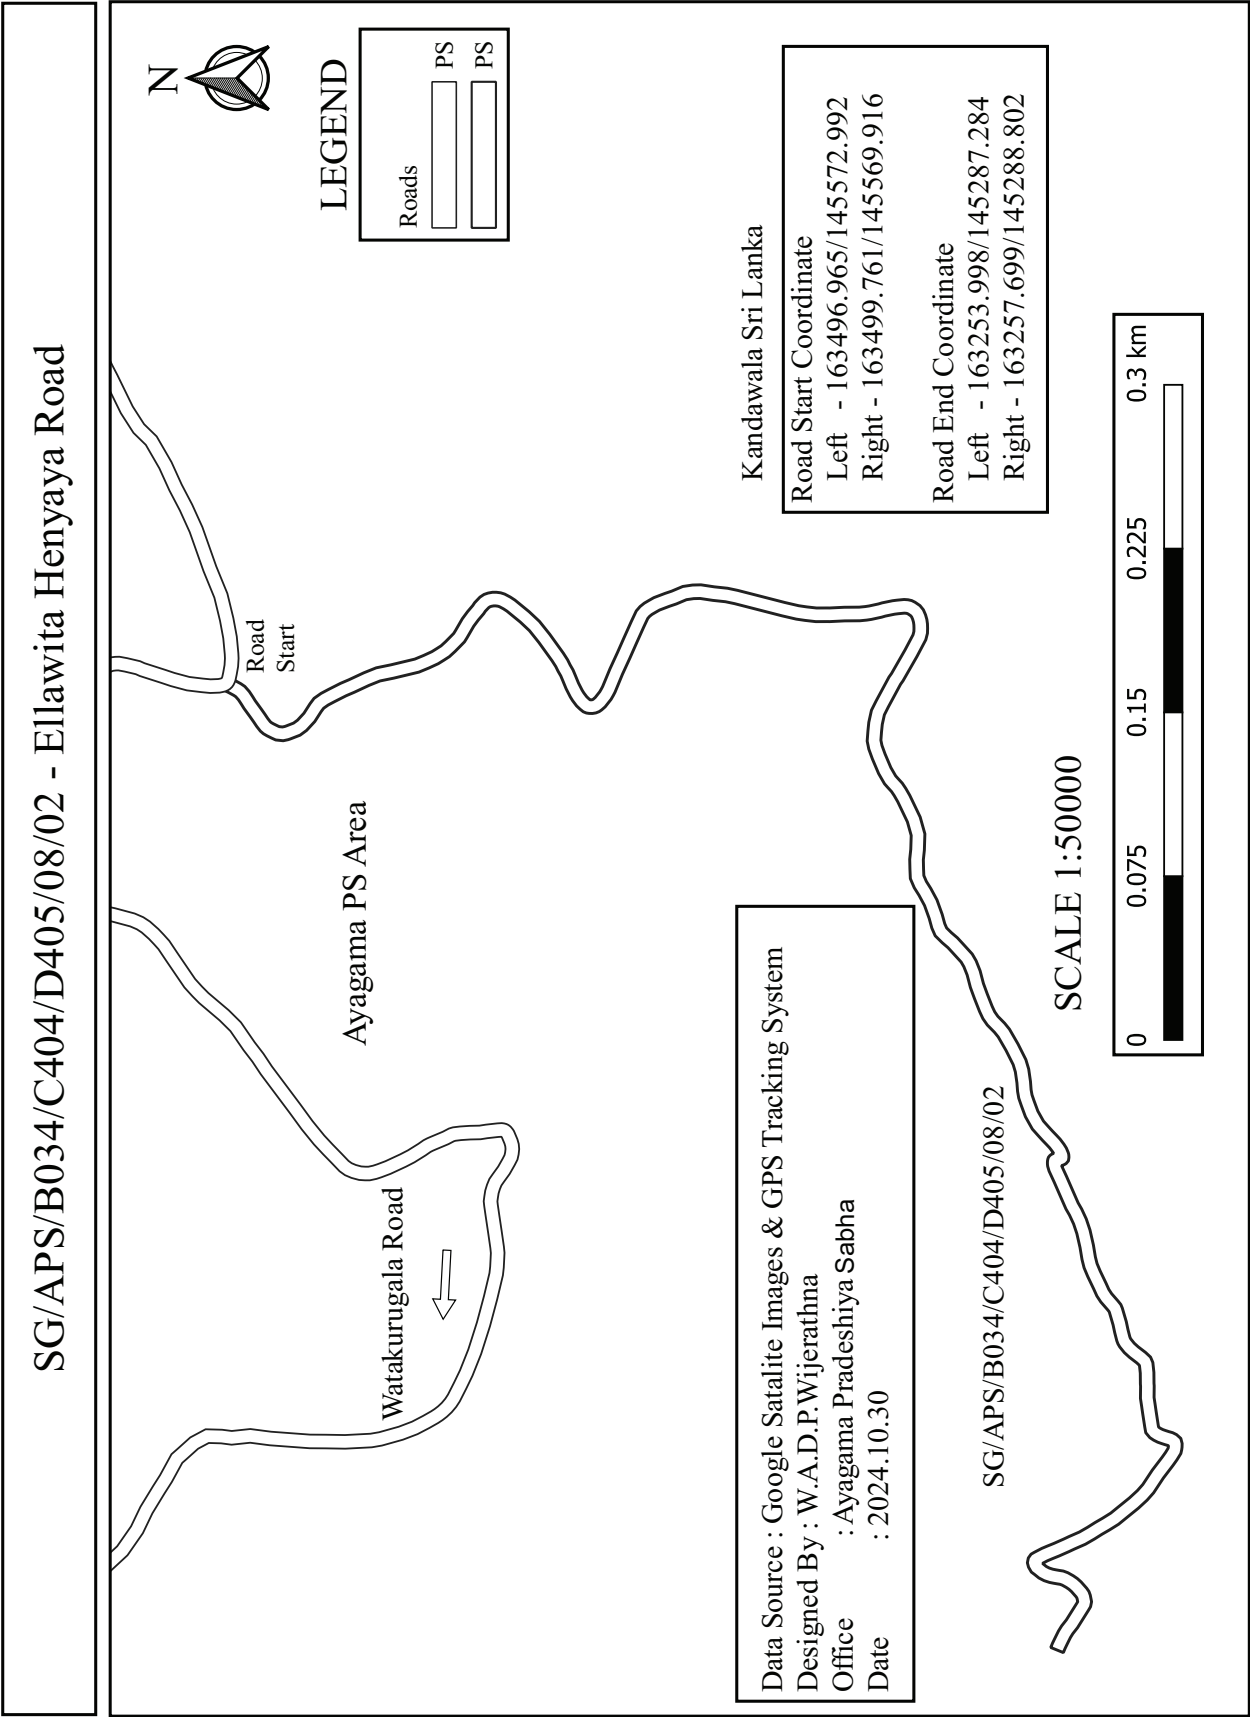


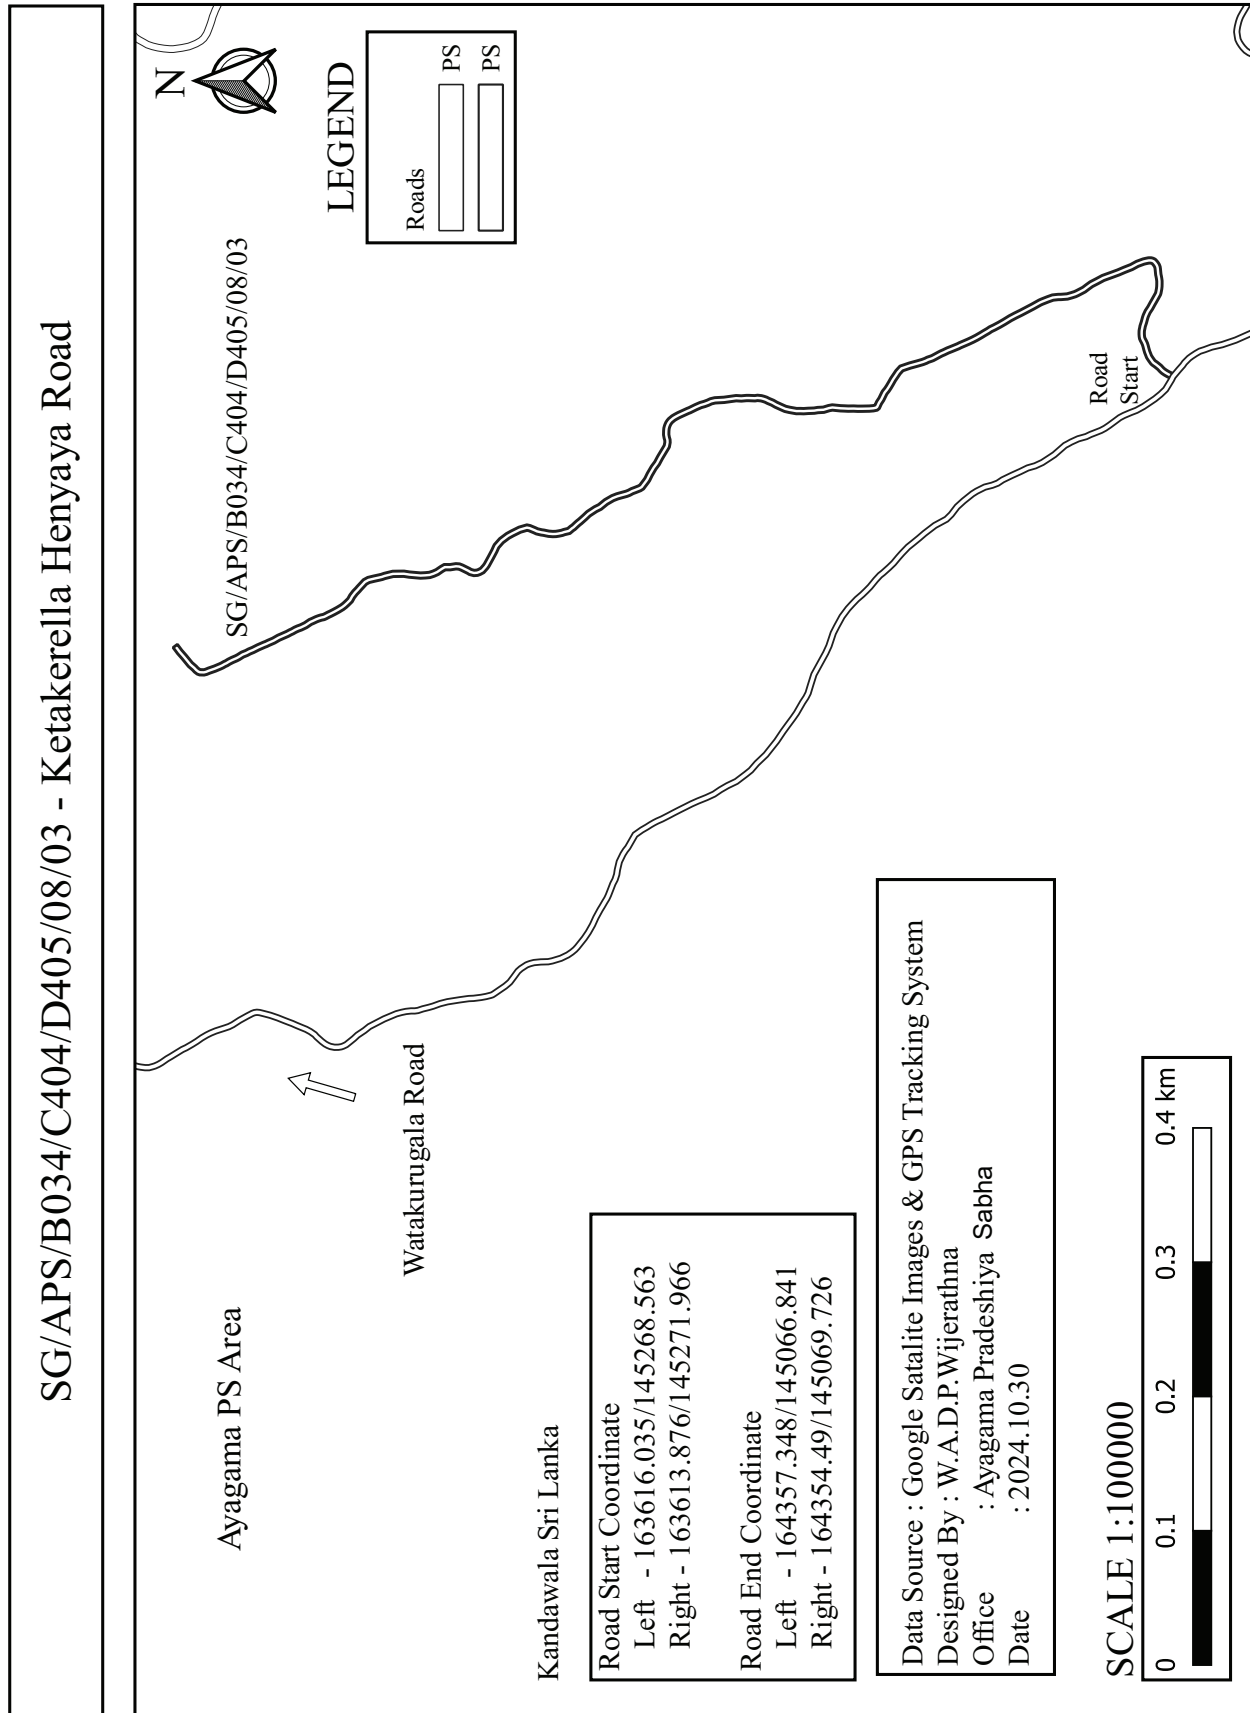

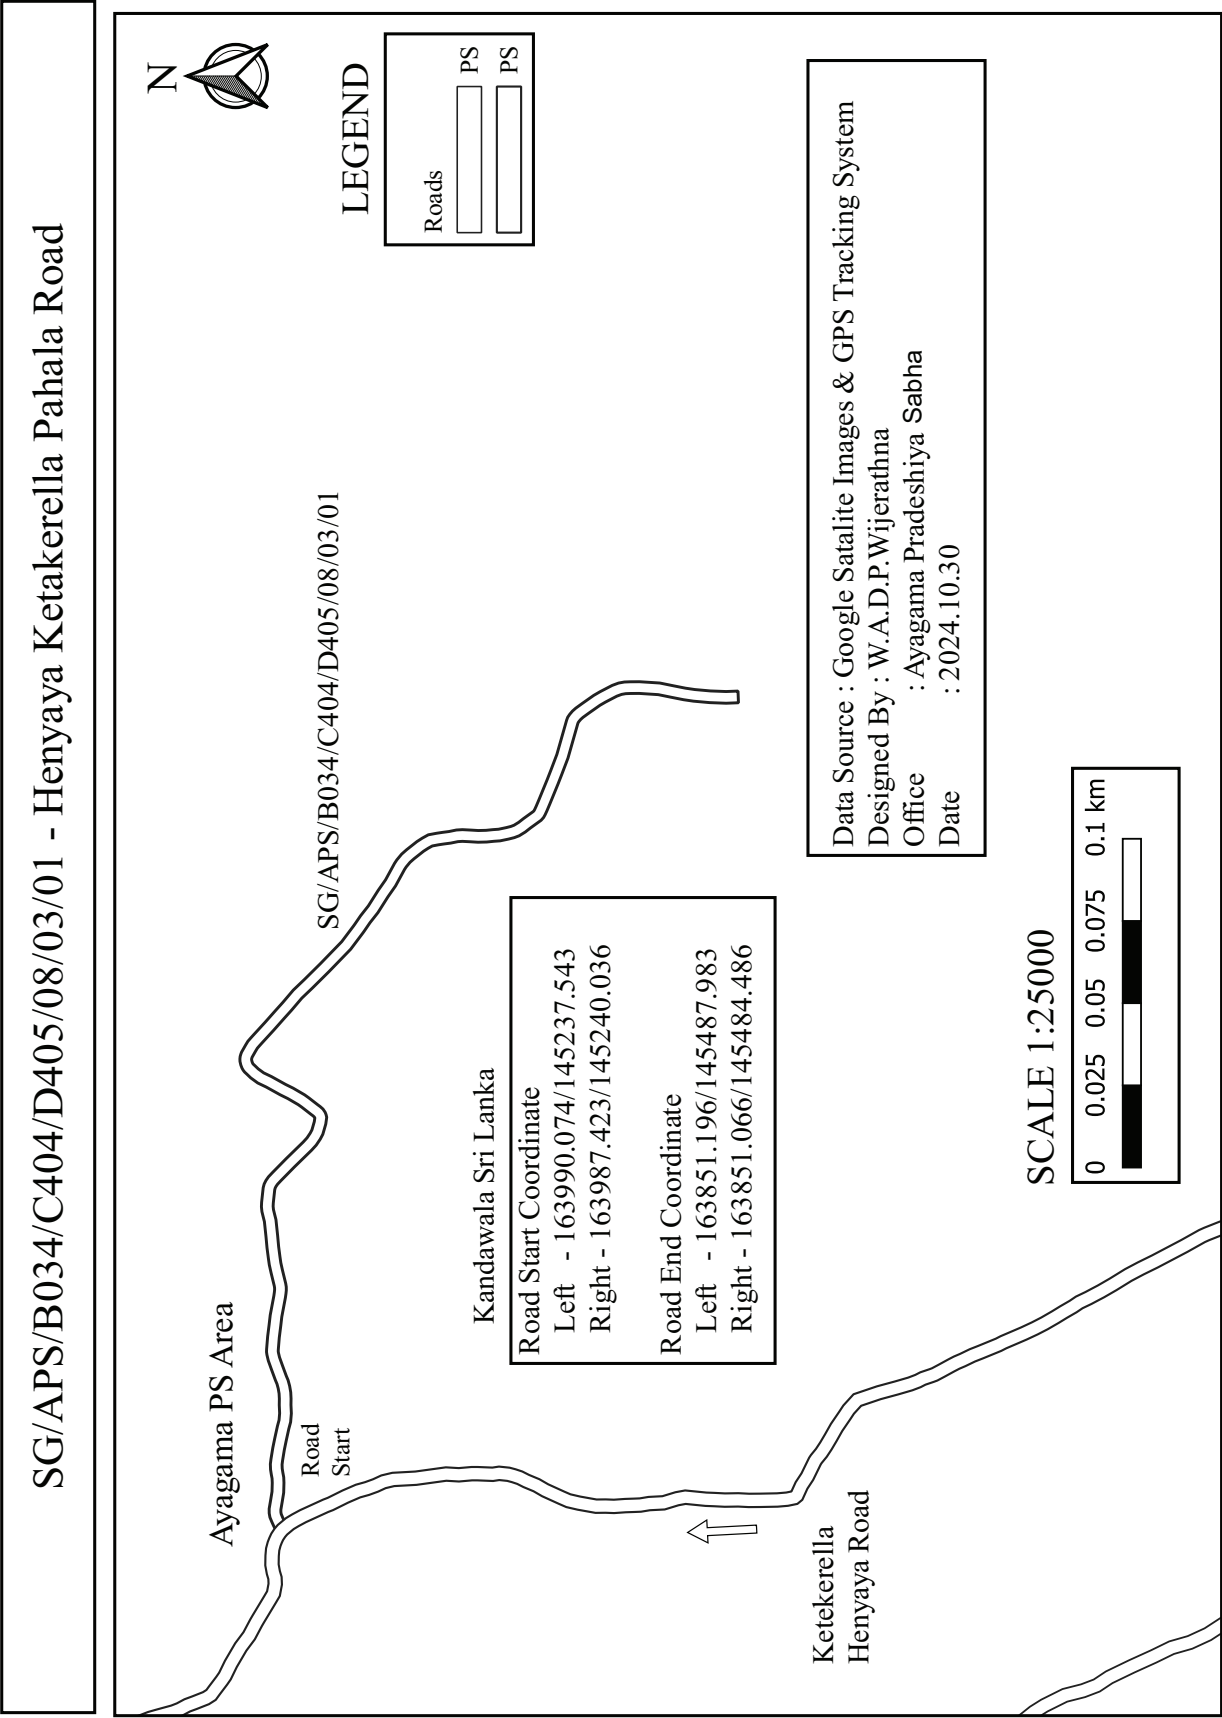

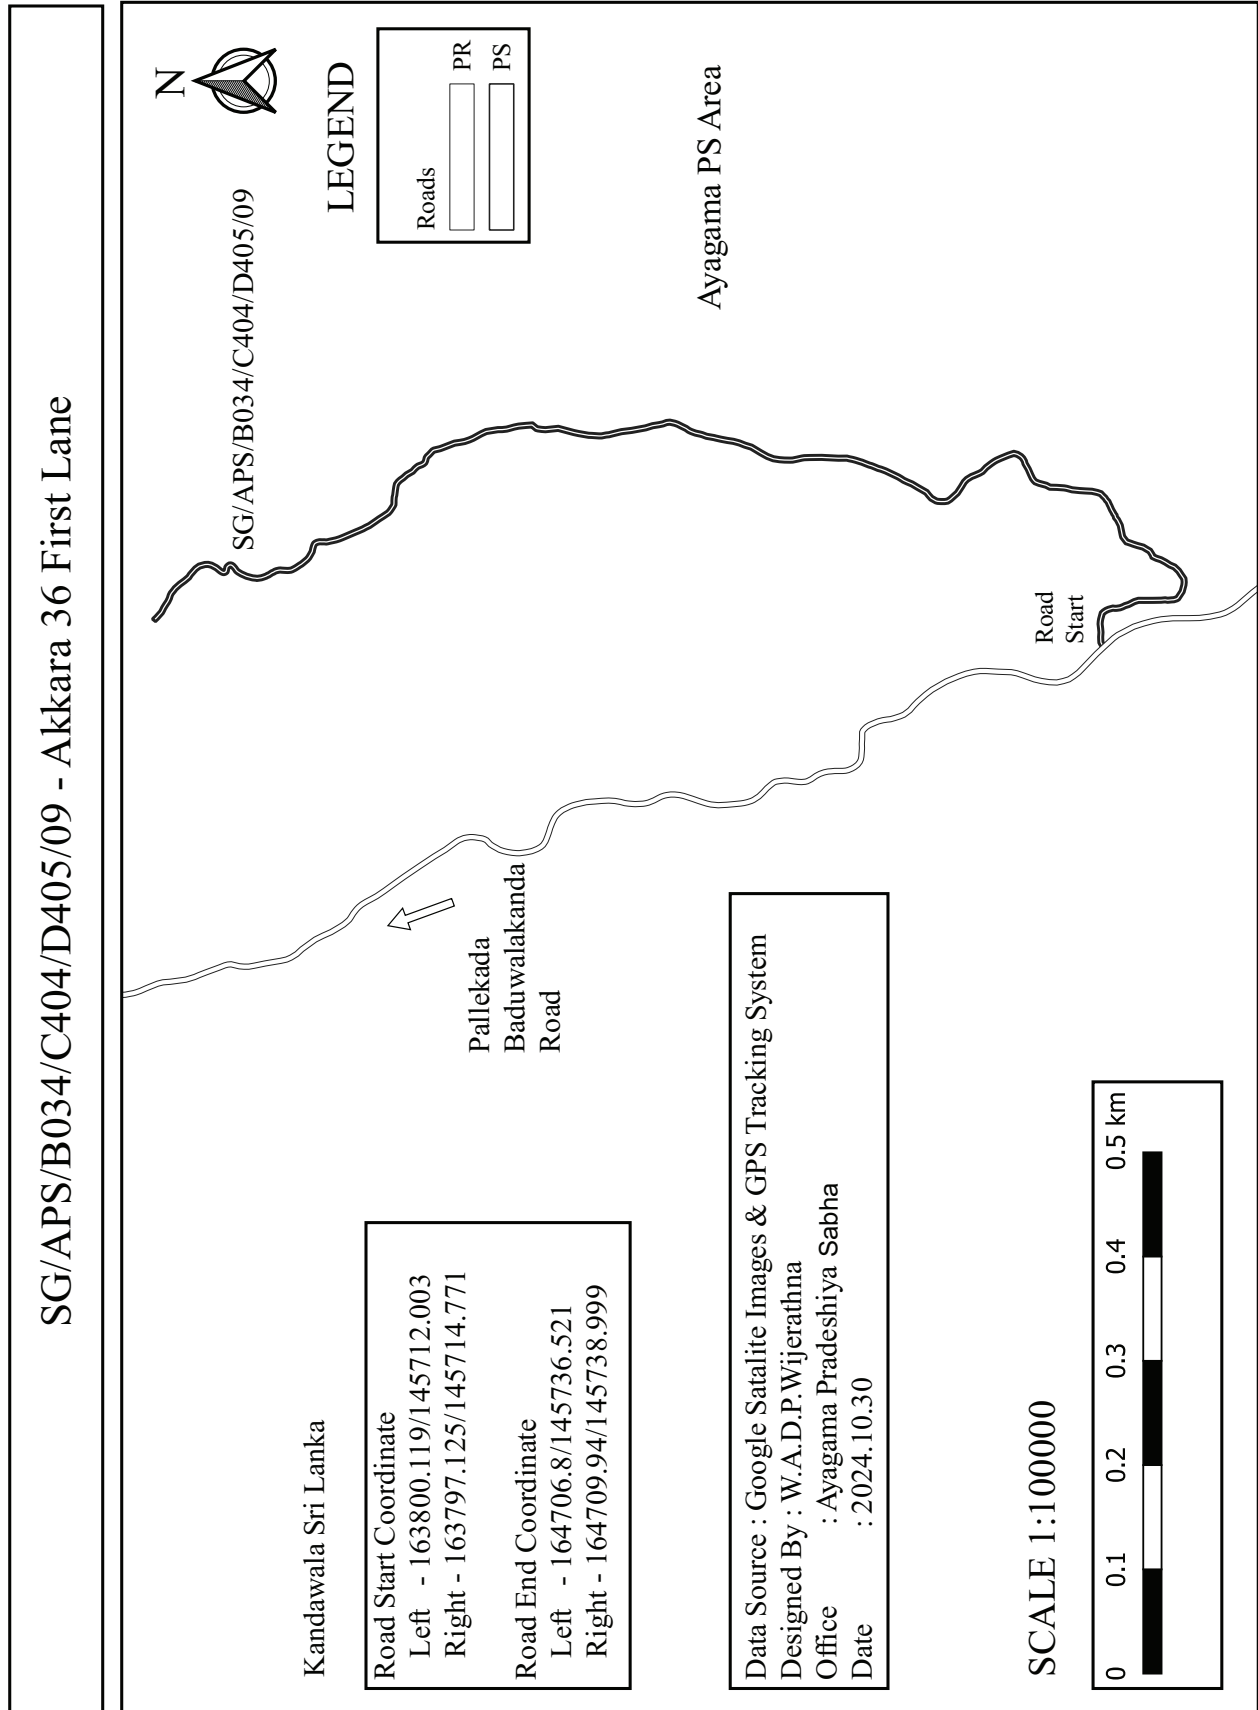

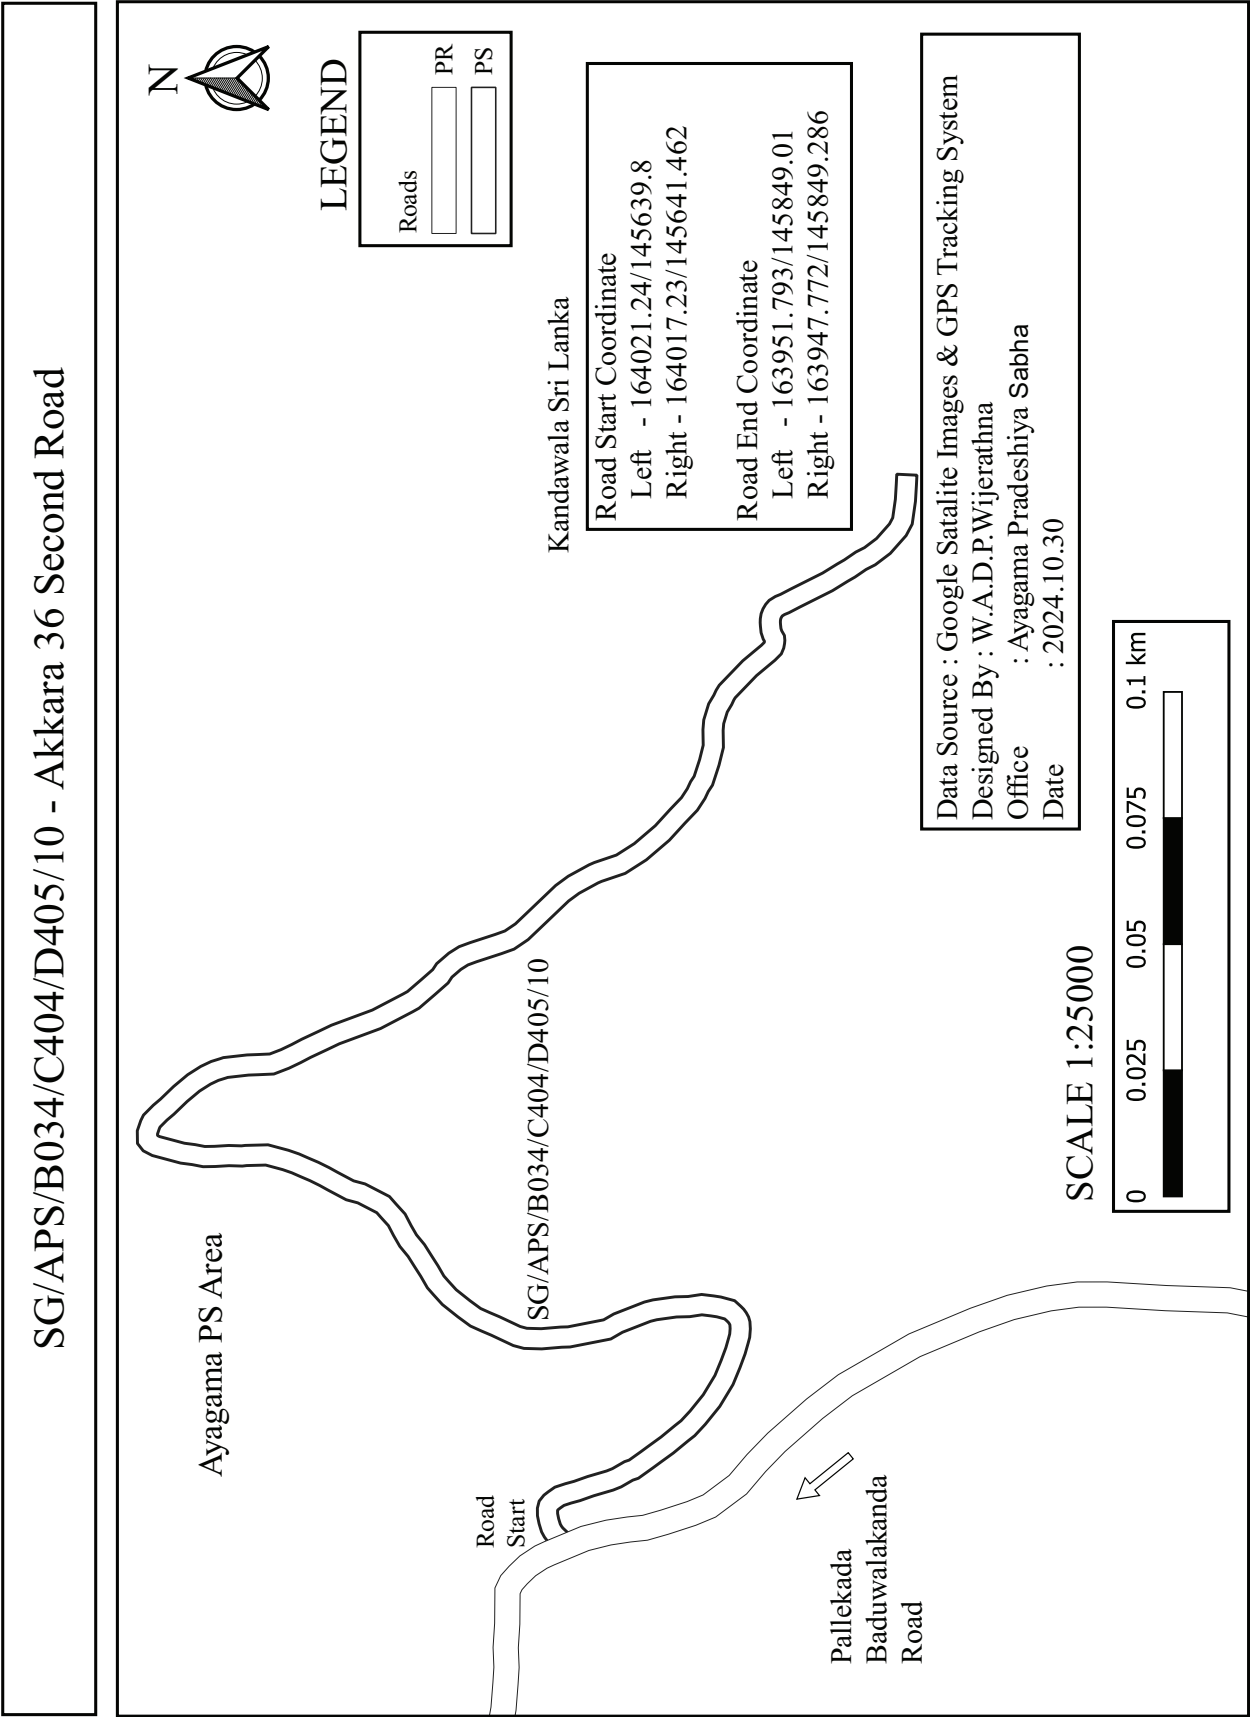

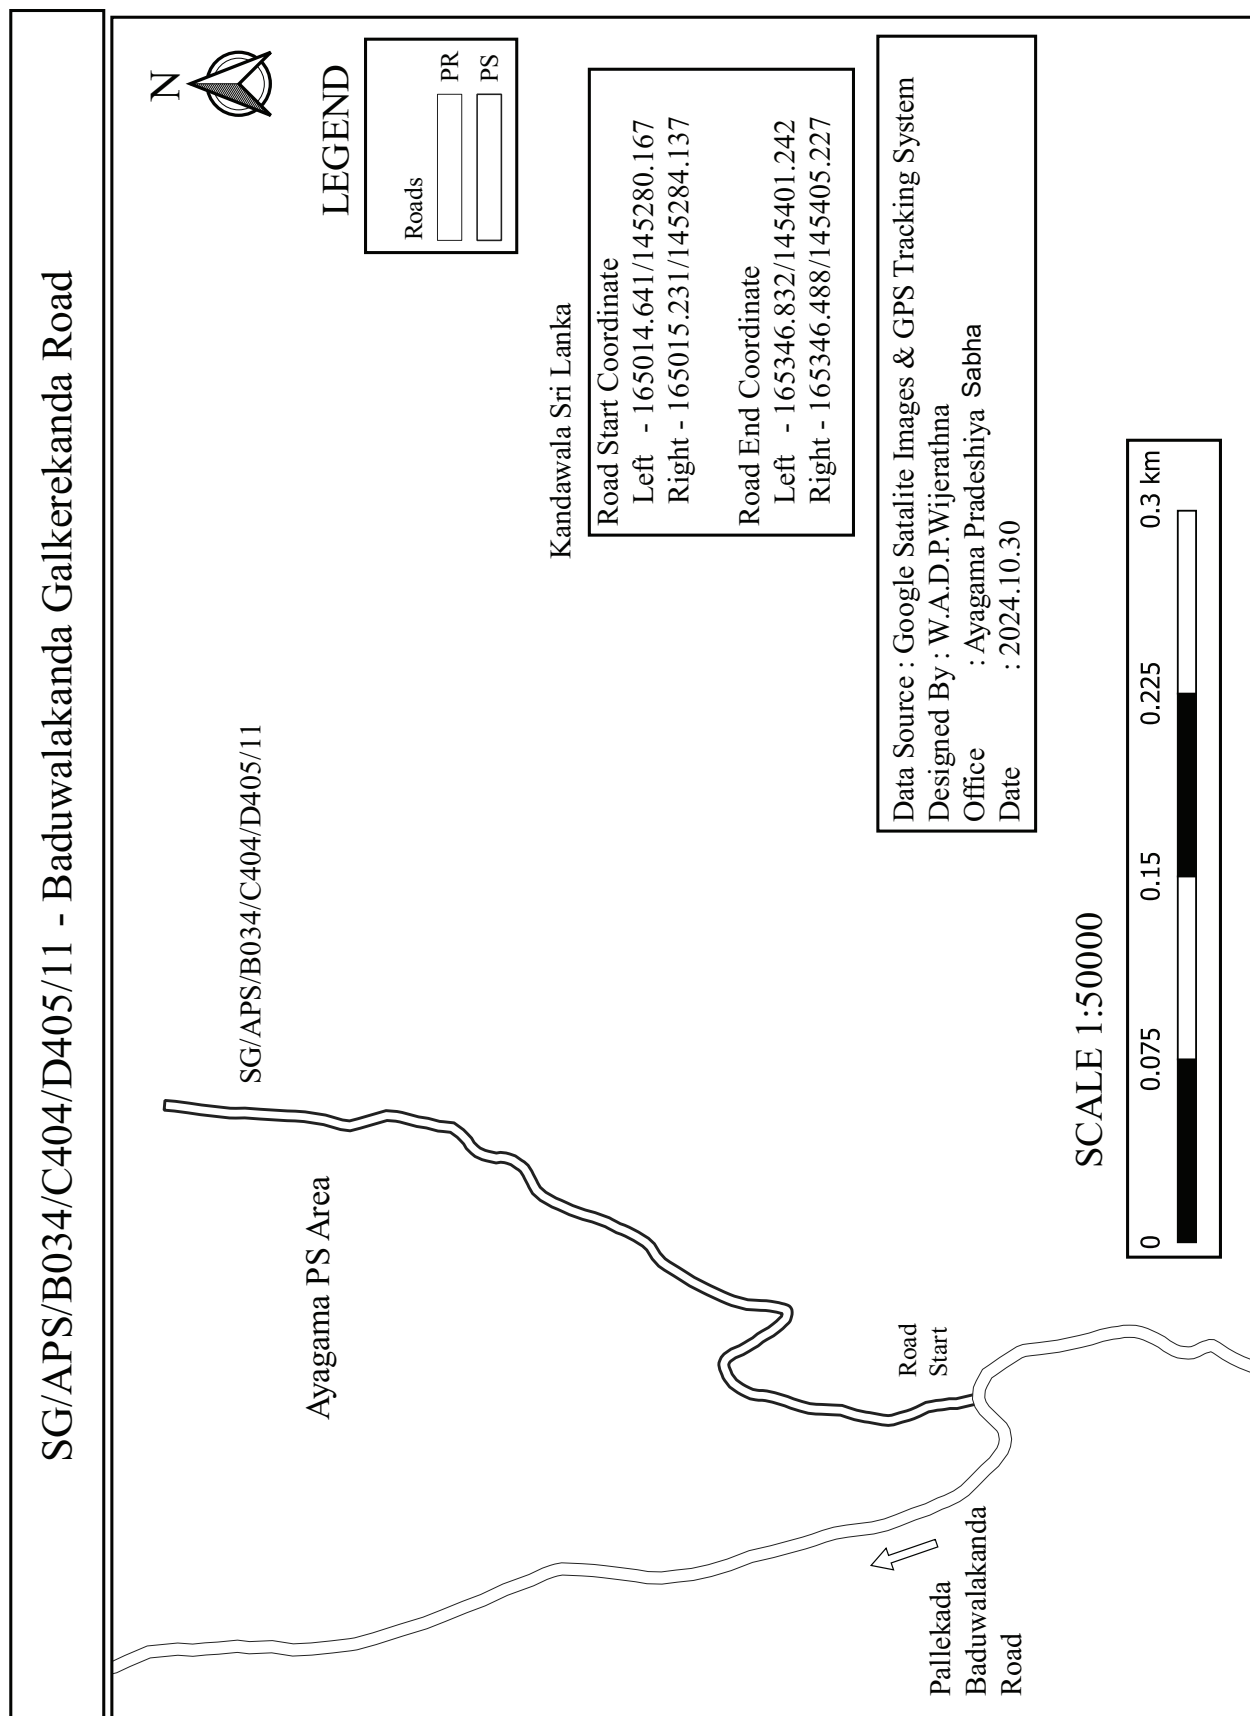

SG/APS/B034/C404/D405/11/01

Ayagama PS Area

N

LEGEND

Roads

PS

PS

Kandawala Sri Lanka

Road Start Coordinate

Left - 165158.3/145353.973

Right - 165152.821/145351.331

Road End Coordinate

Left - 166198.582/145939.273

Right - 166195.509/145937.524

Data Source : Google Satalite Images & GPS Tracking System

Designed By : W.A.D.P.Wijerathna

Office : Ayagama Pradeshiya Sabha

Date : 2024.10.30

SCALE 1:100000


0 0.1 0.2 0.3 0.4 0.5 km


Baduwalakanda

Galkerekanda


Road


Road Start

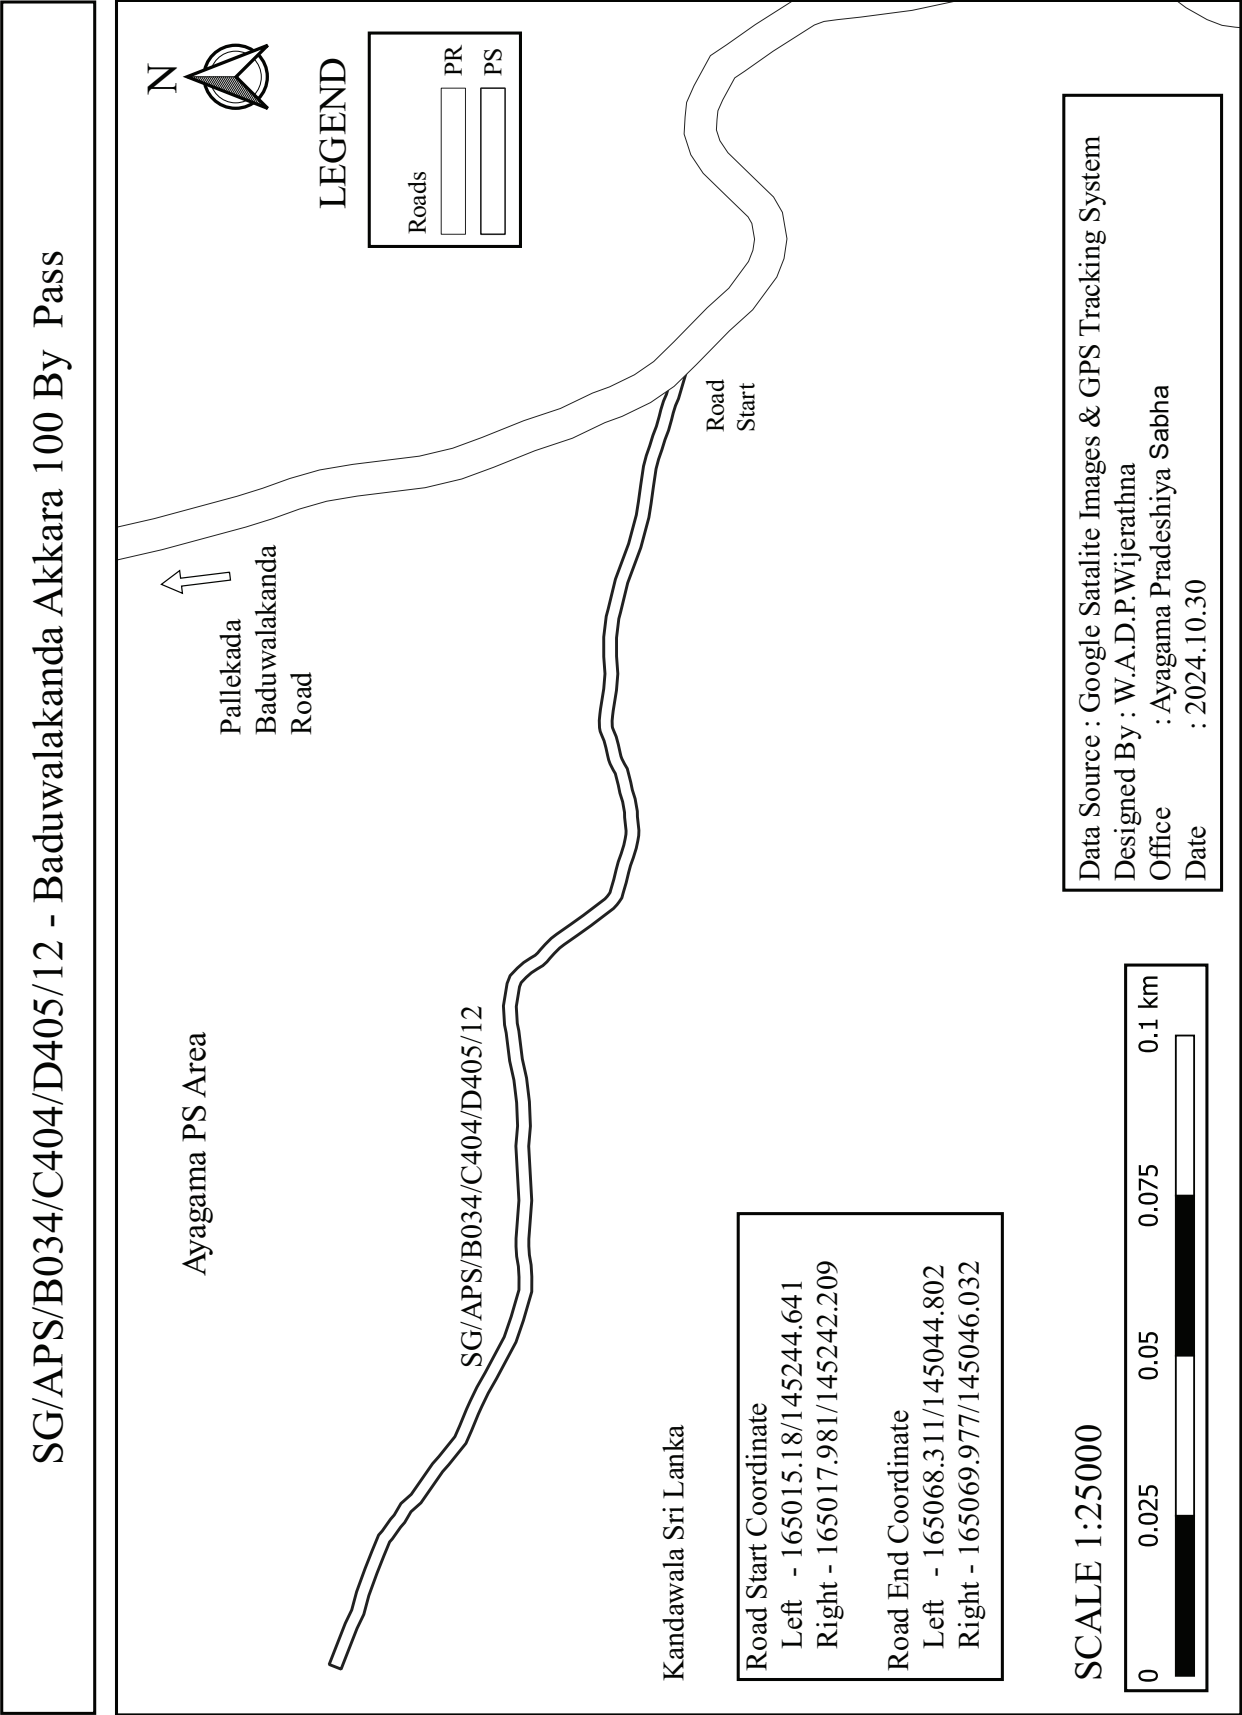


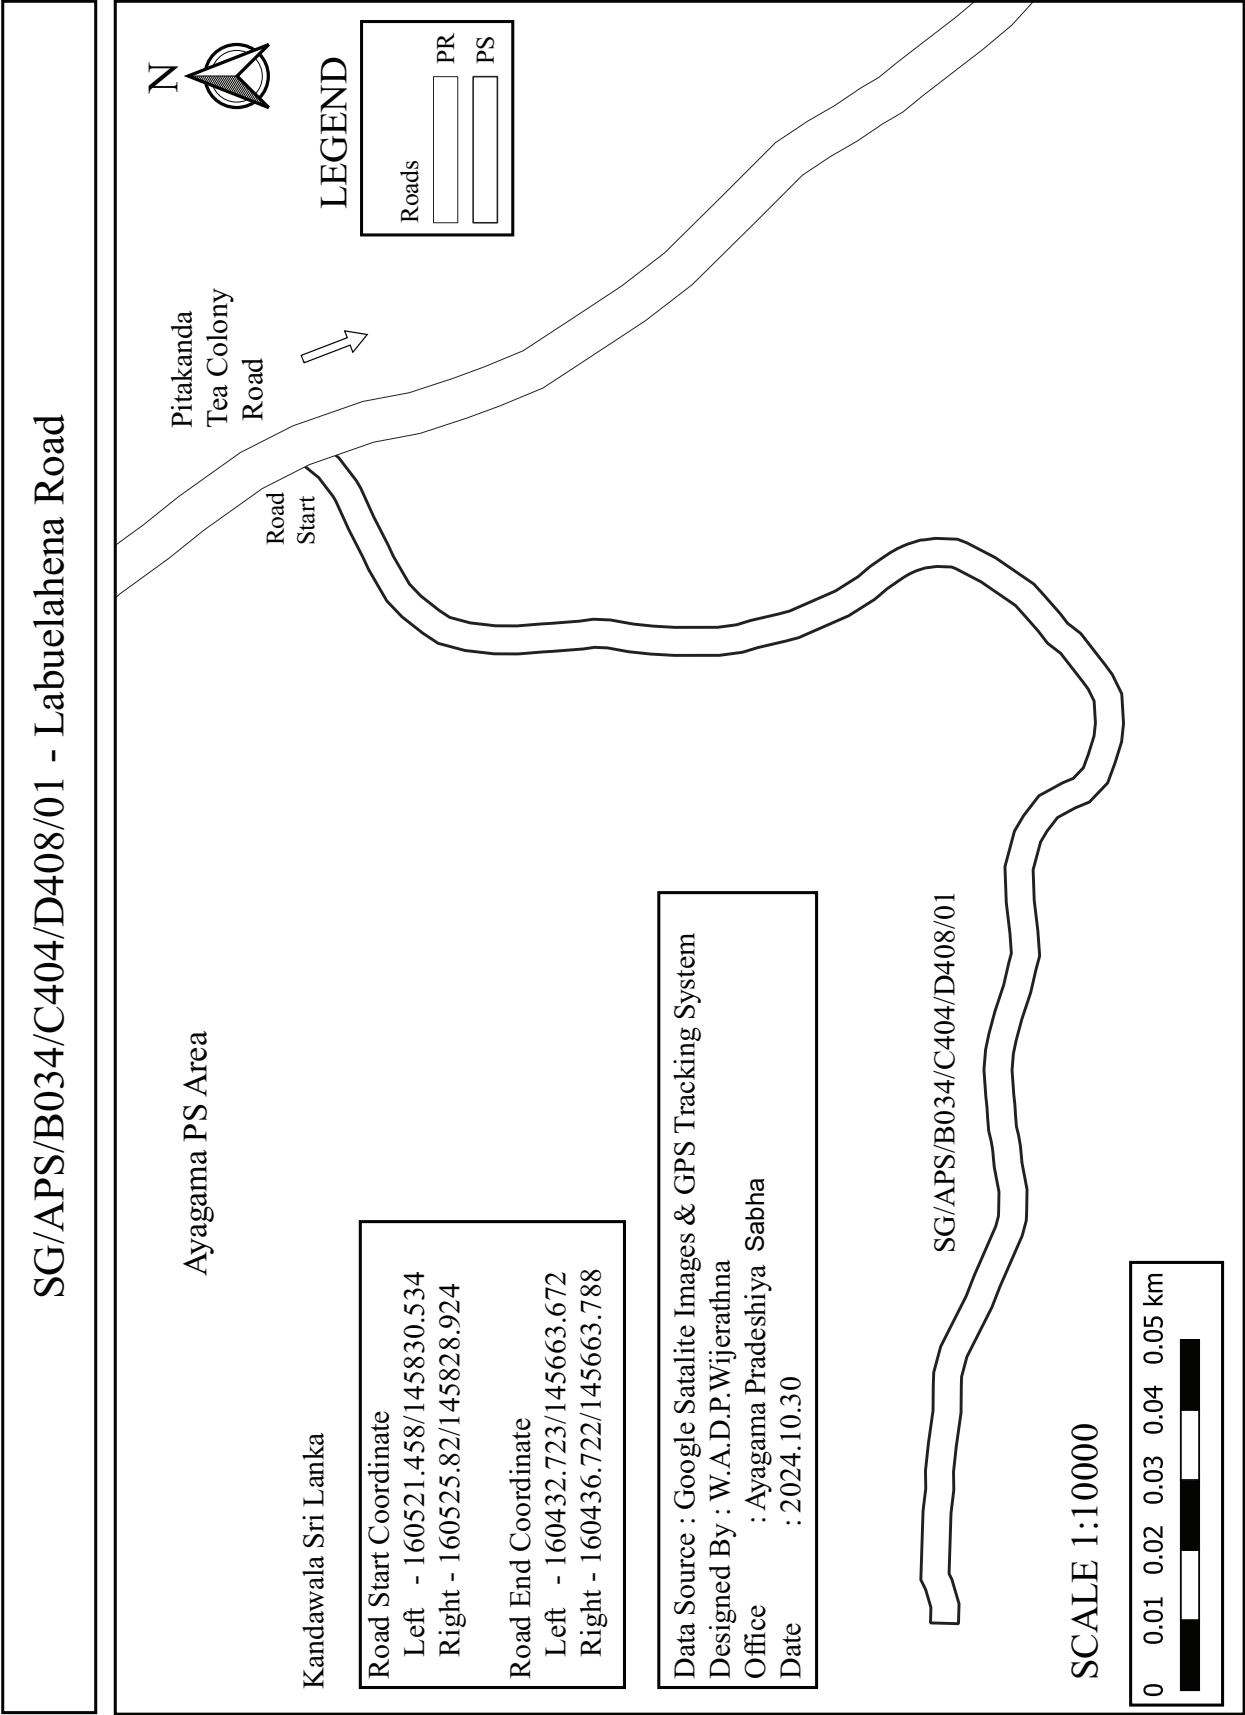


SG/APS/B034/C404/D408/02 - Tea Colony Mahindaramaya Road

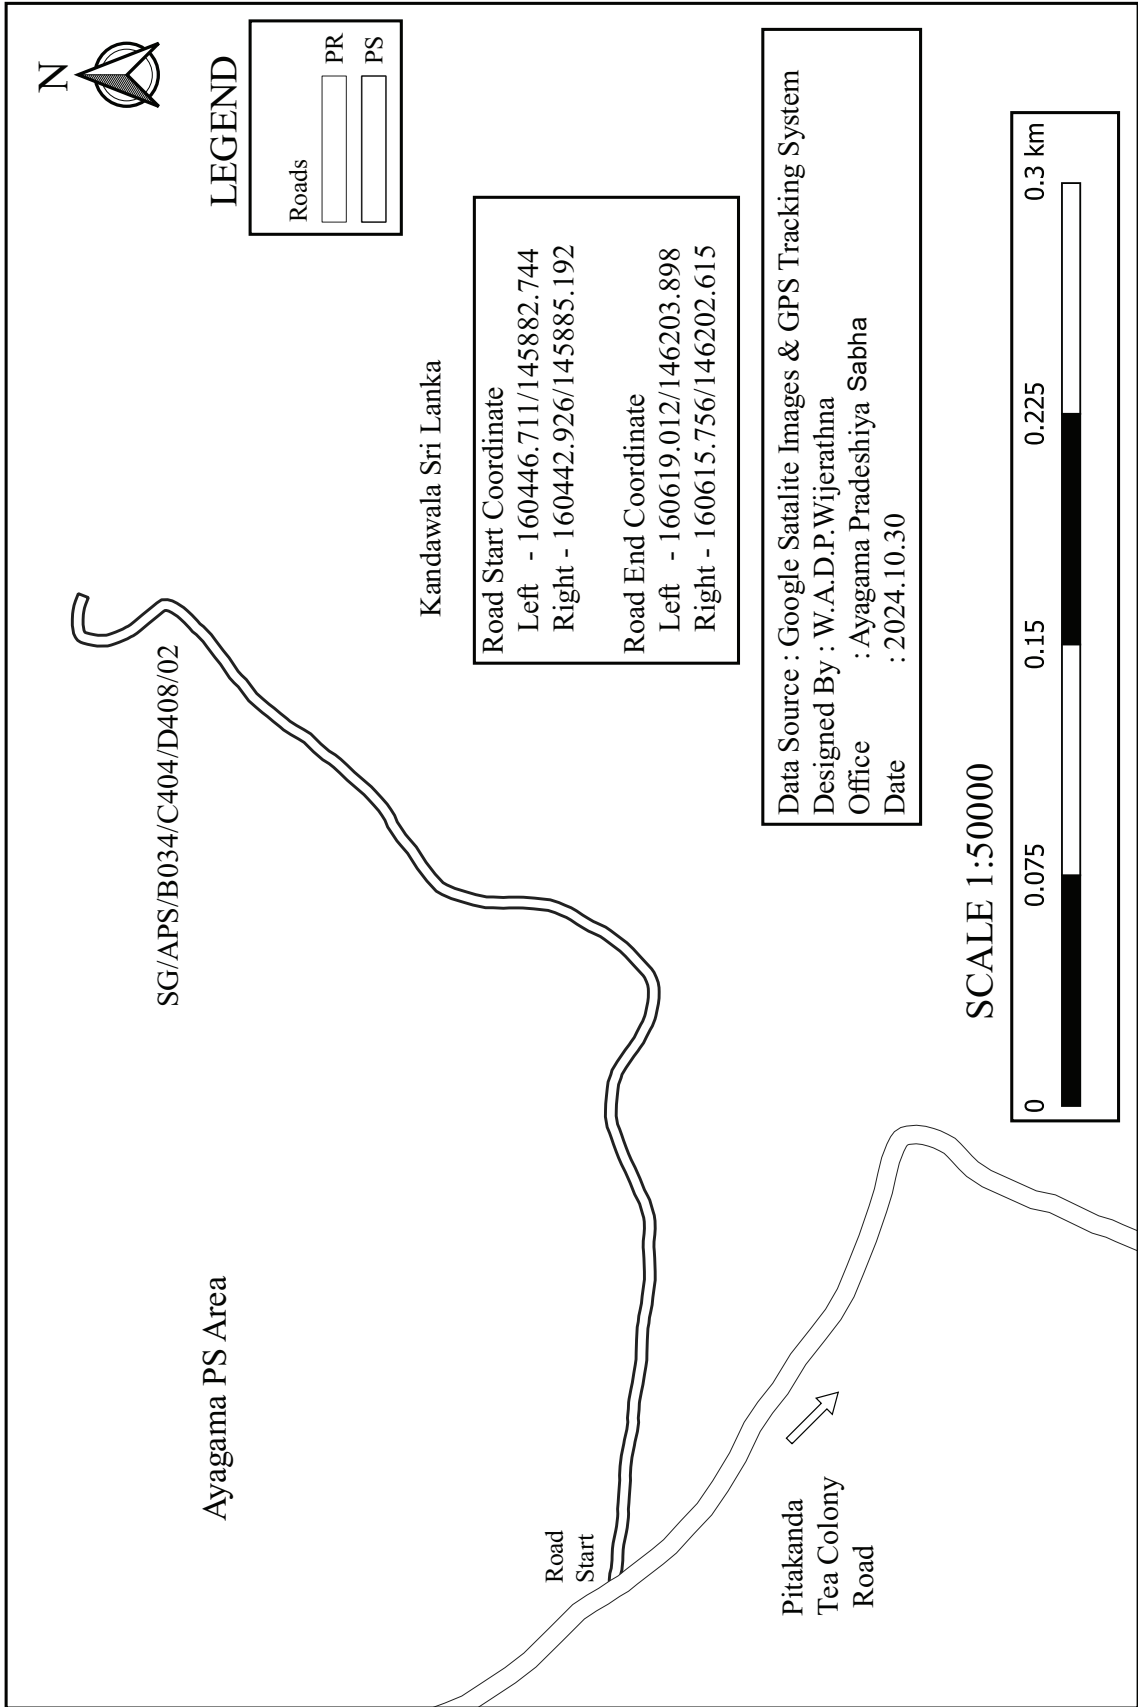


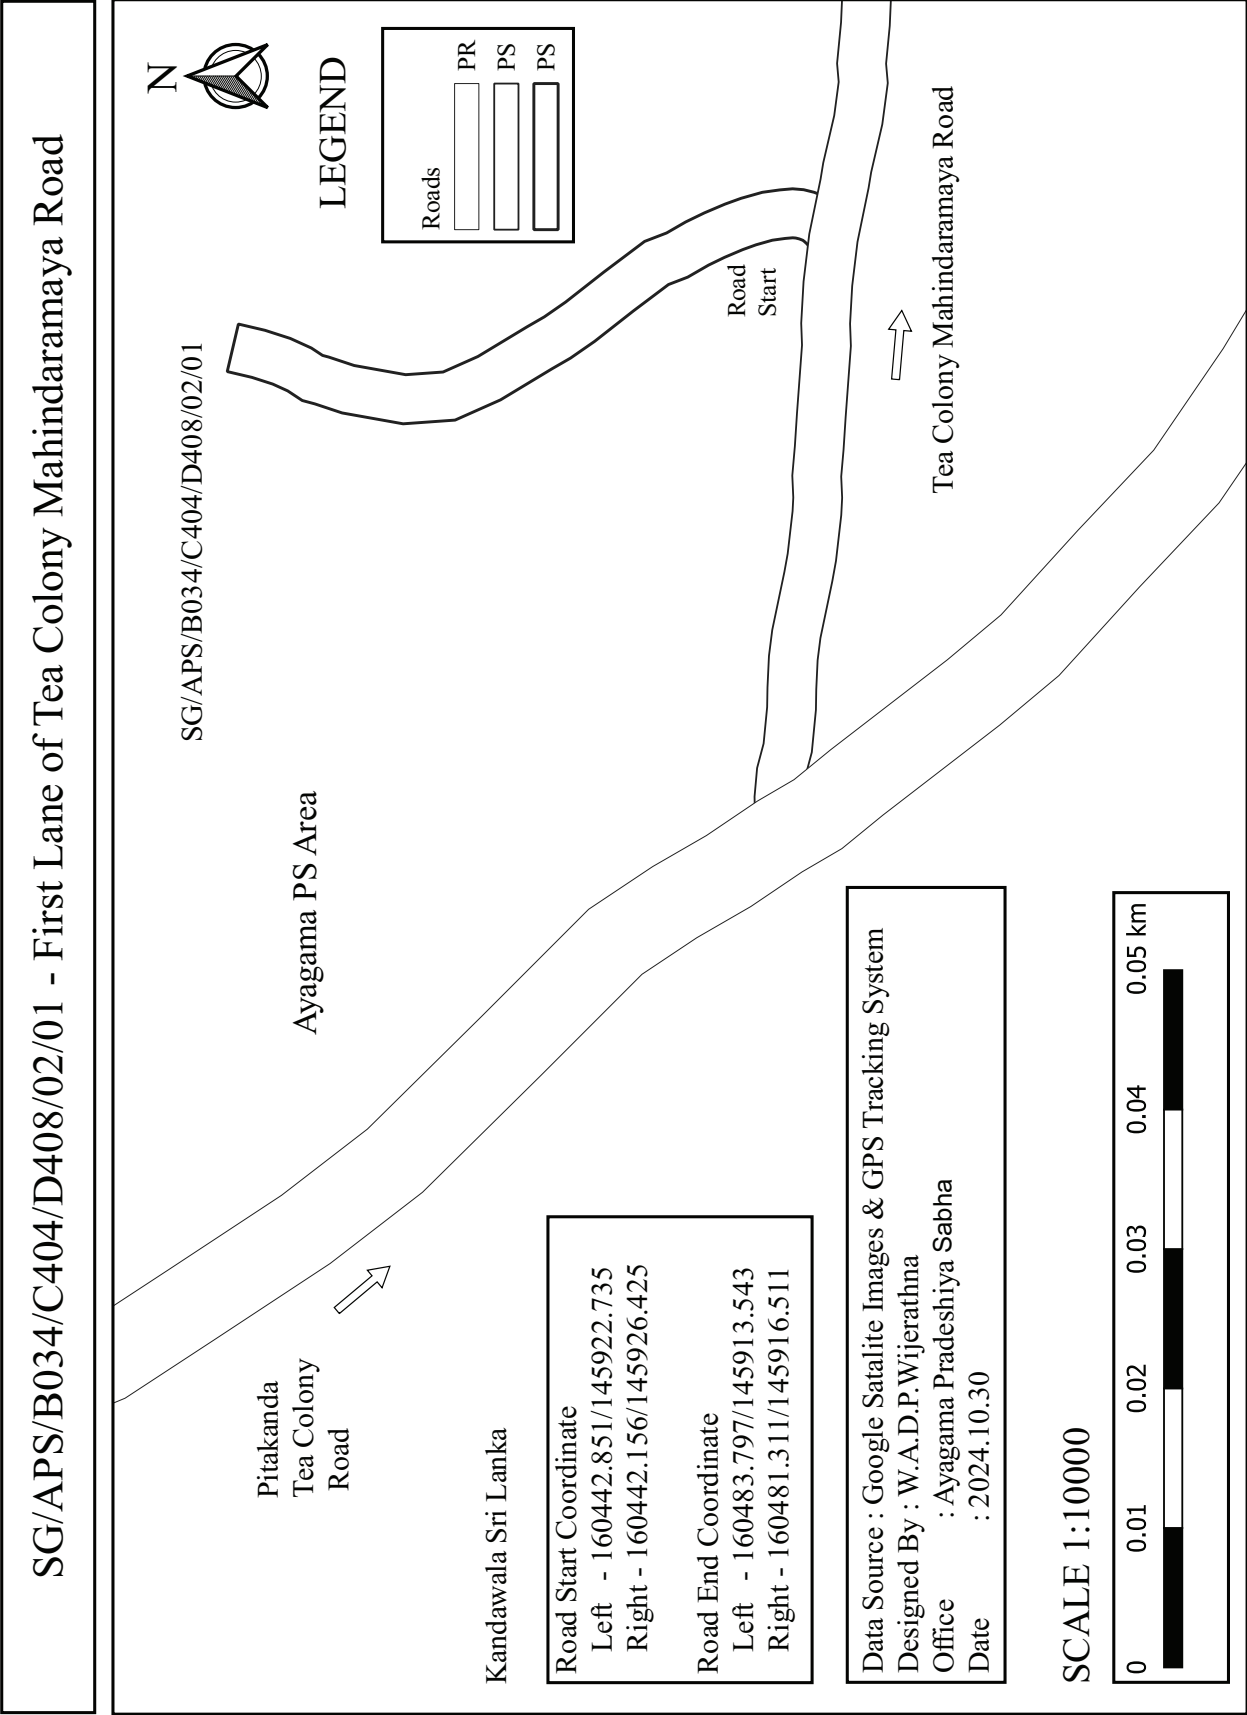


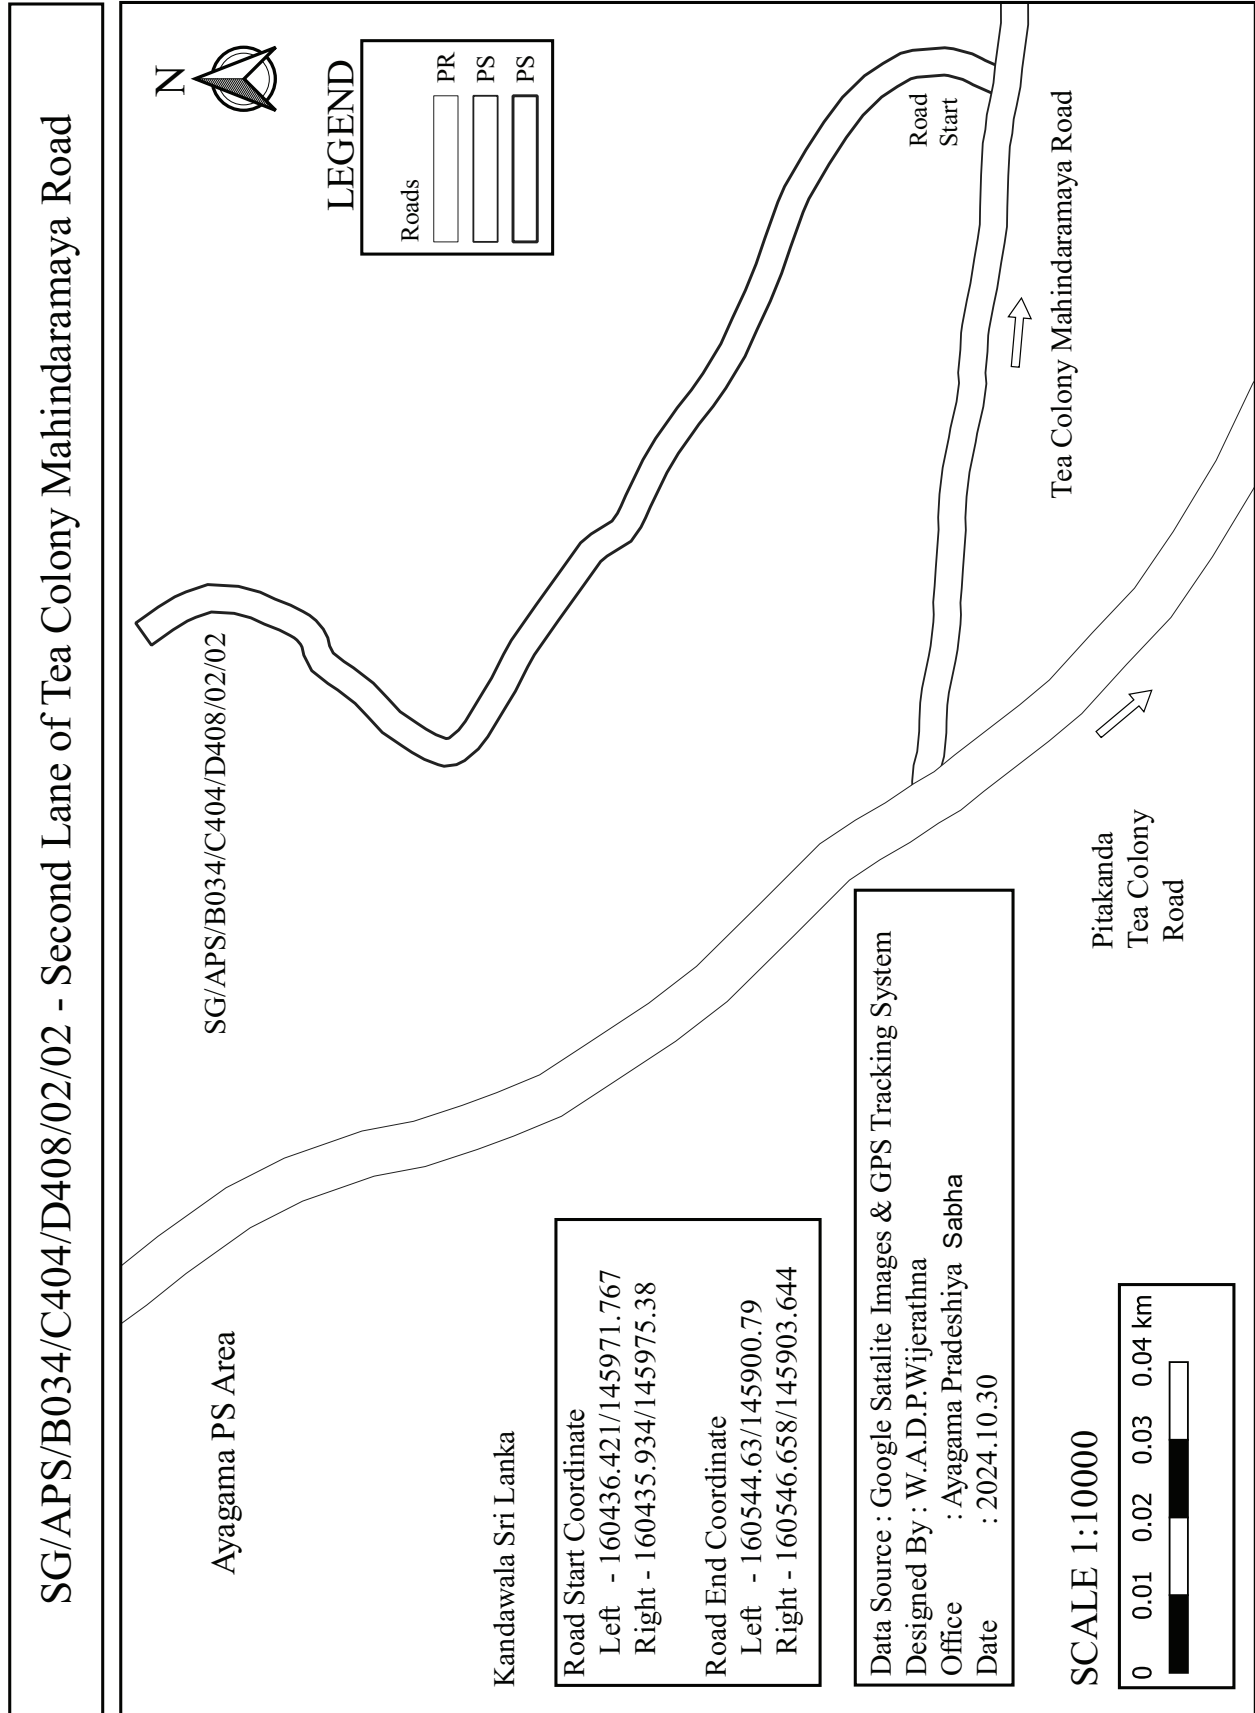


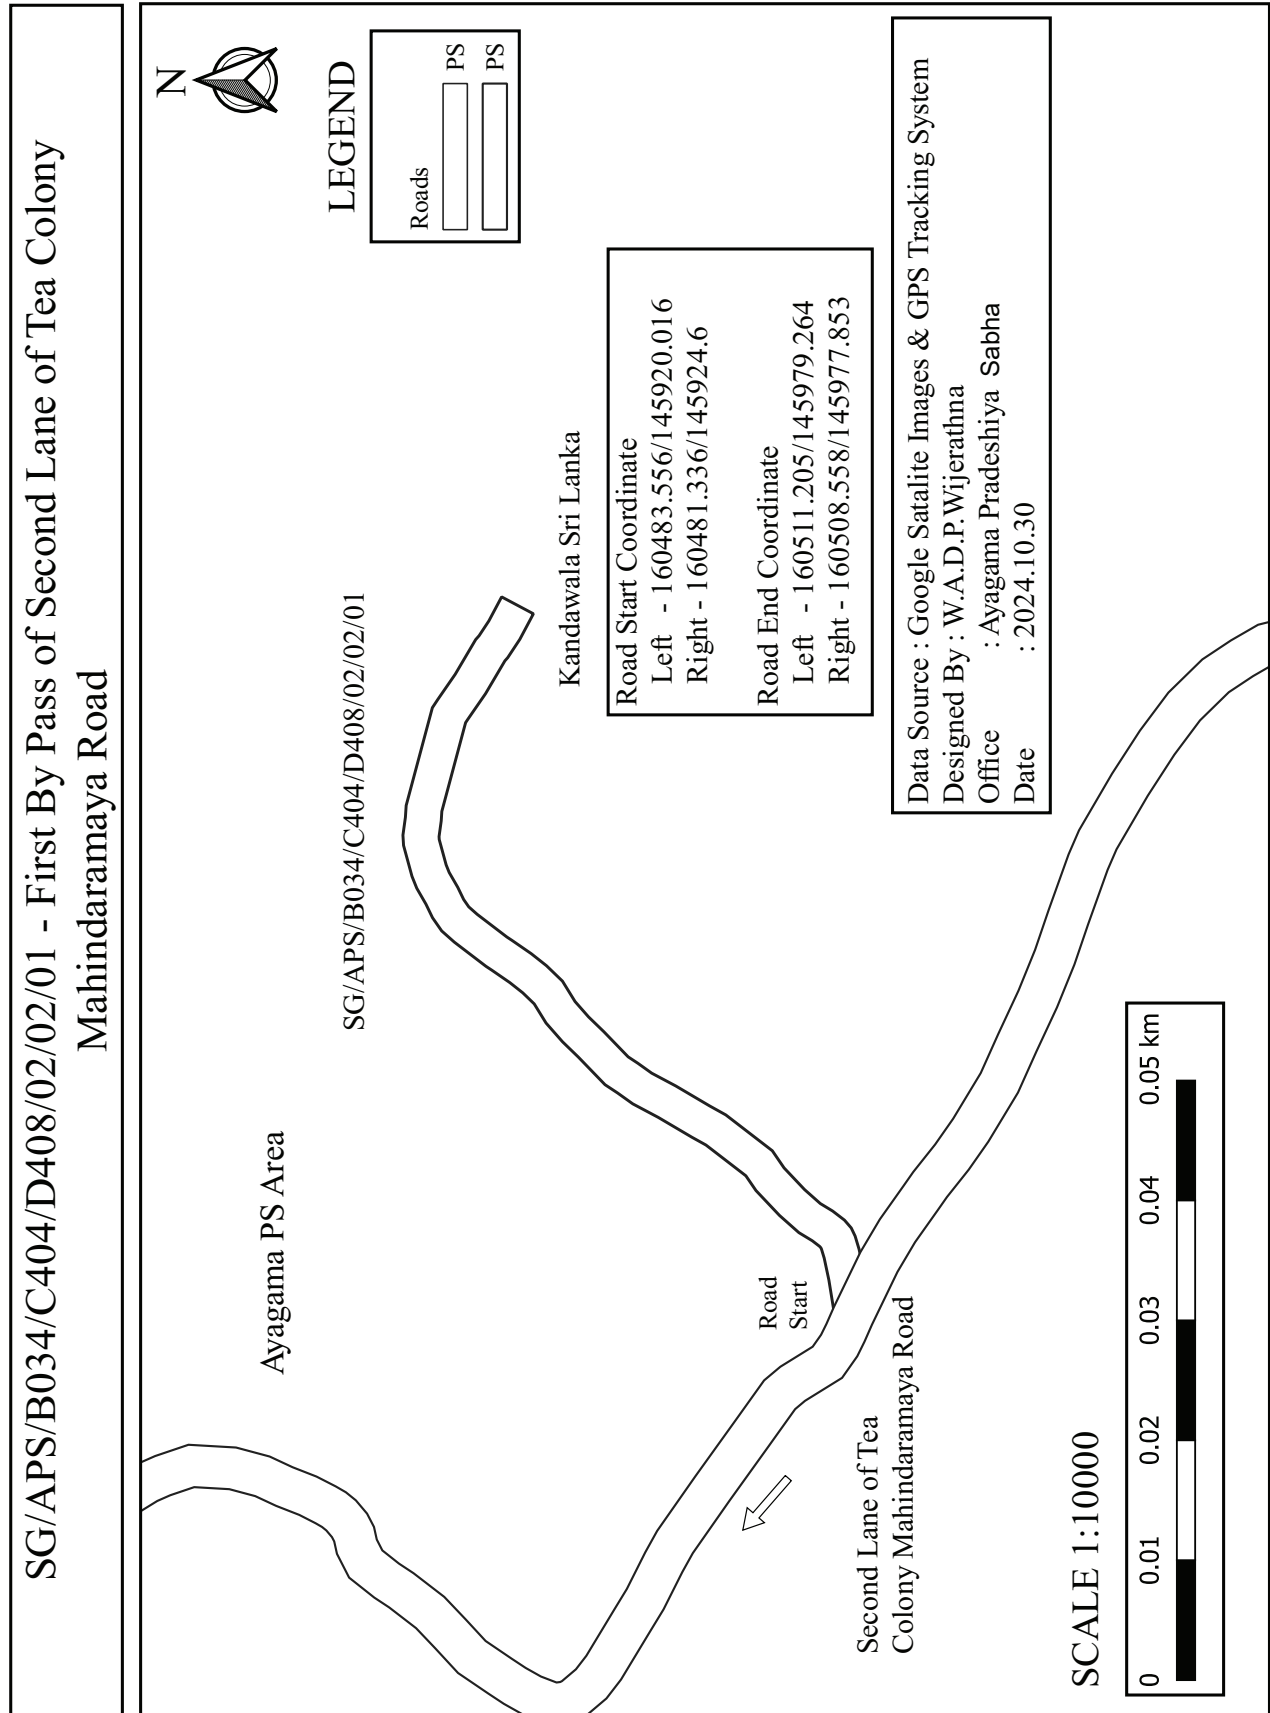



SG/APS/B034/C404/D408/02/03 - Third Lane of Tea Colony Mahindaramaya Road

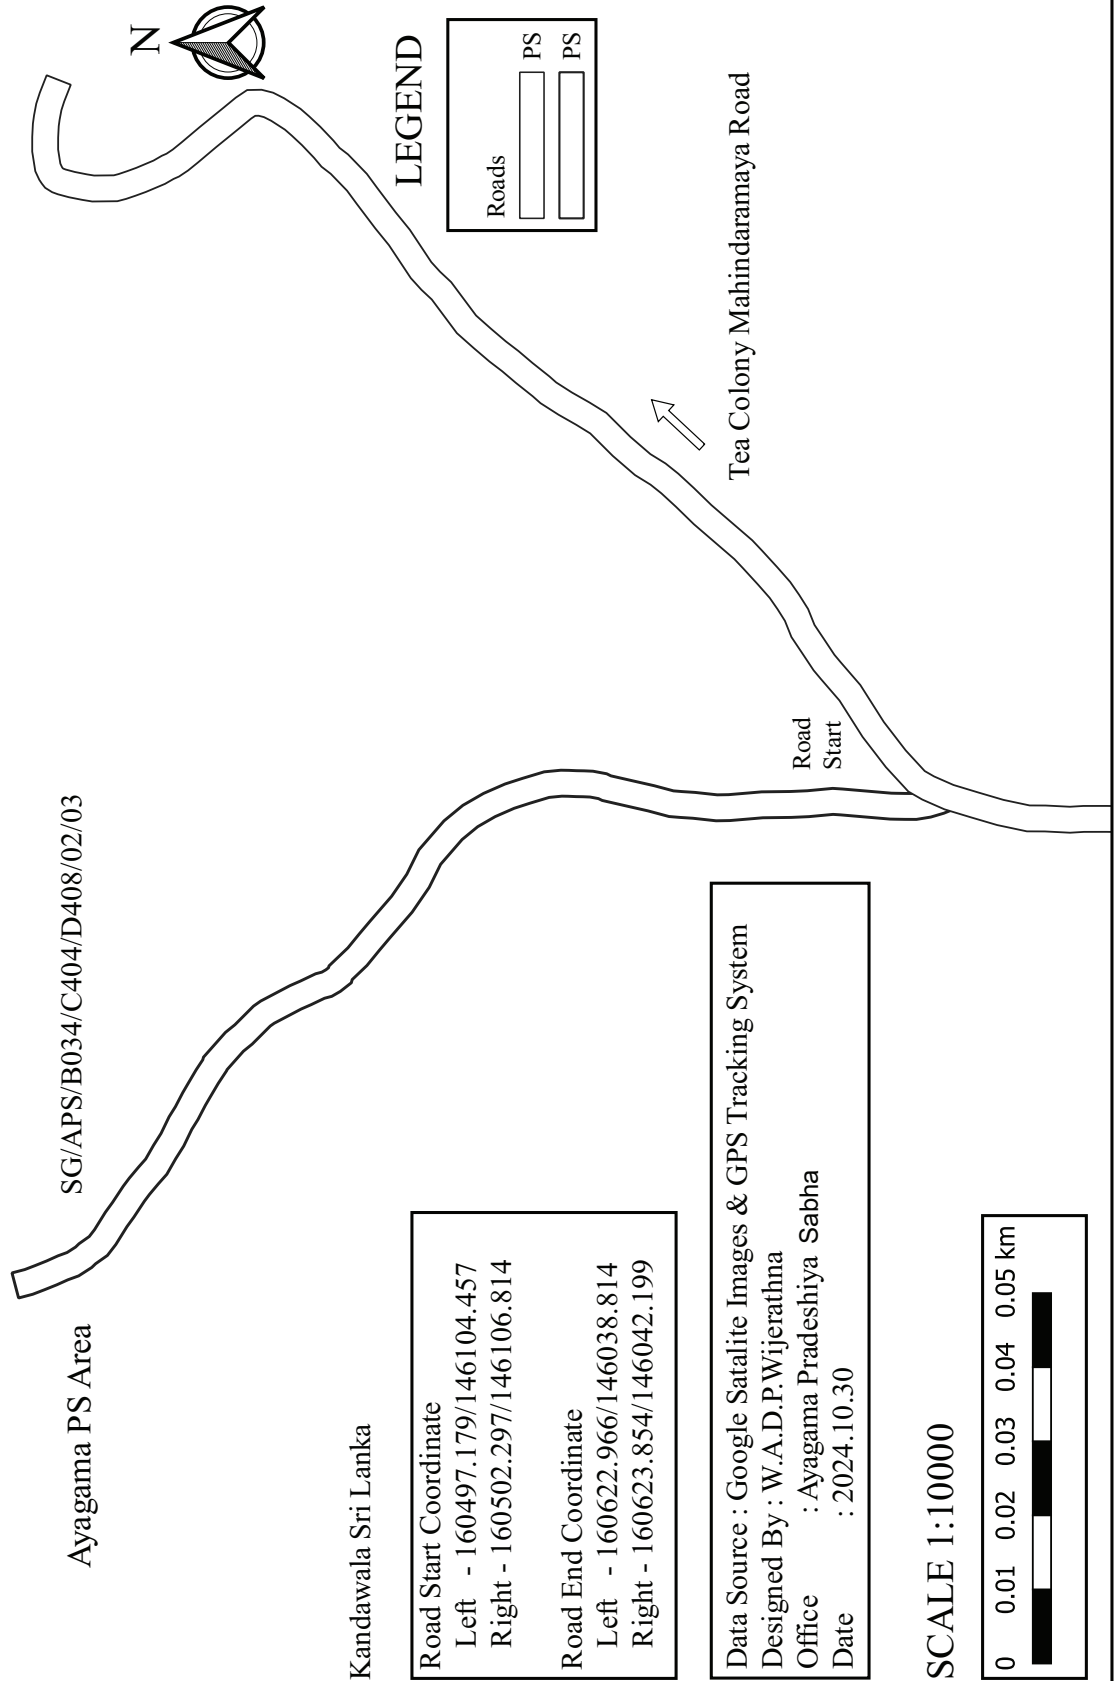


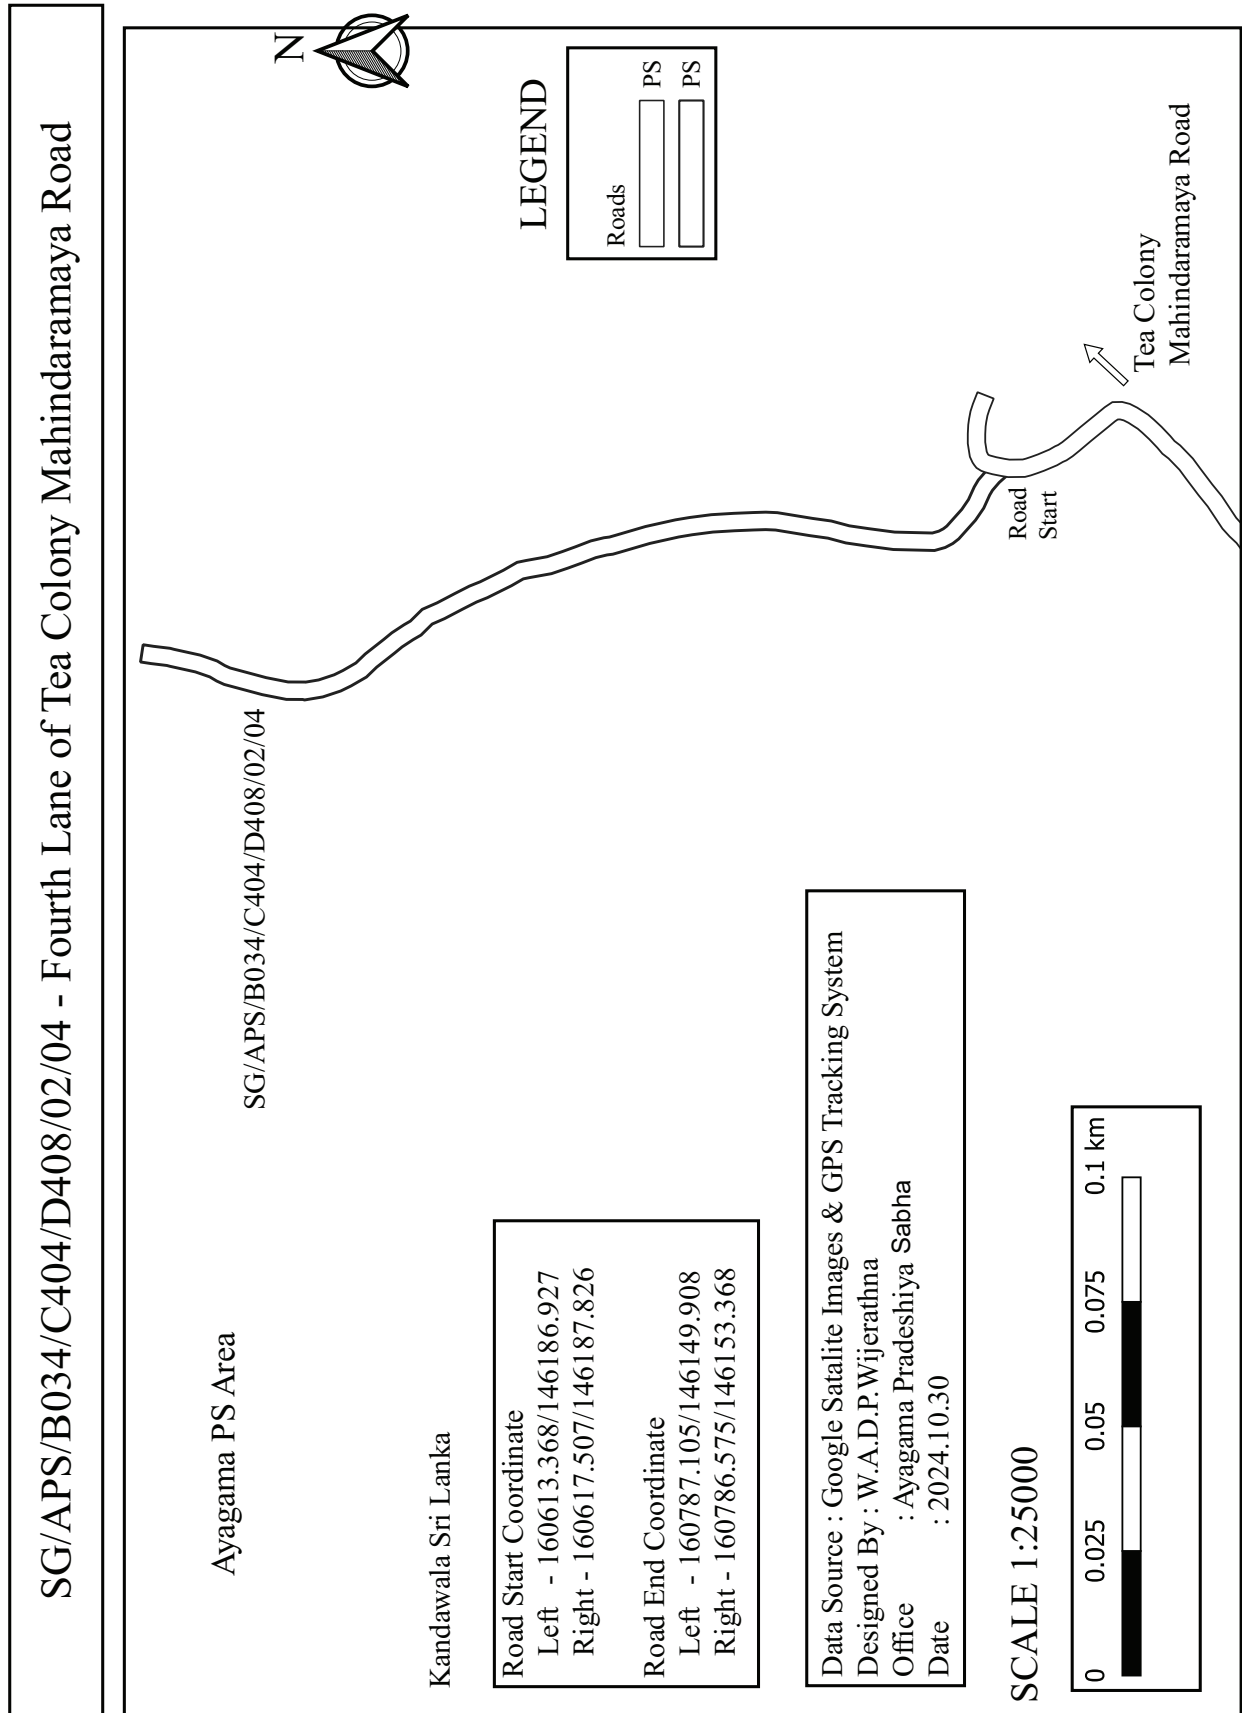


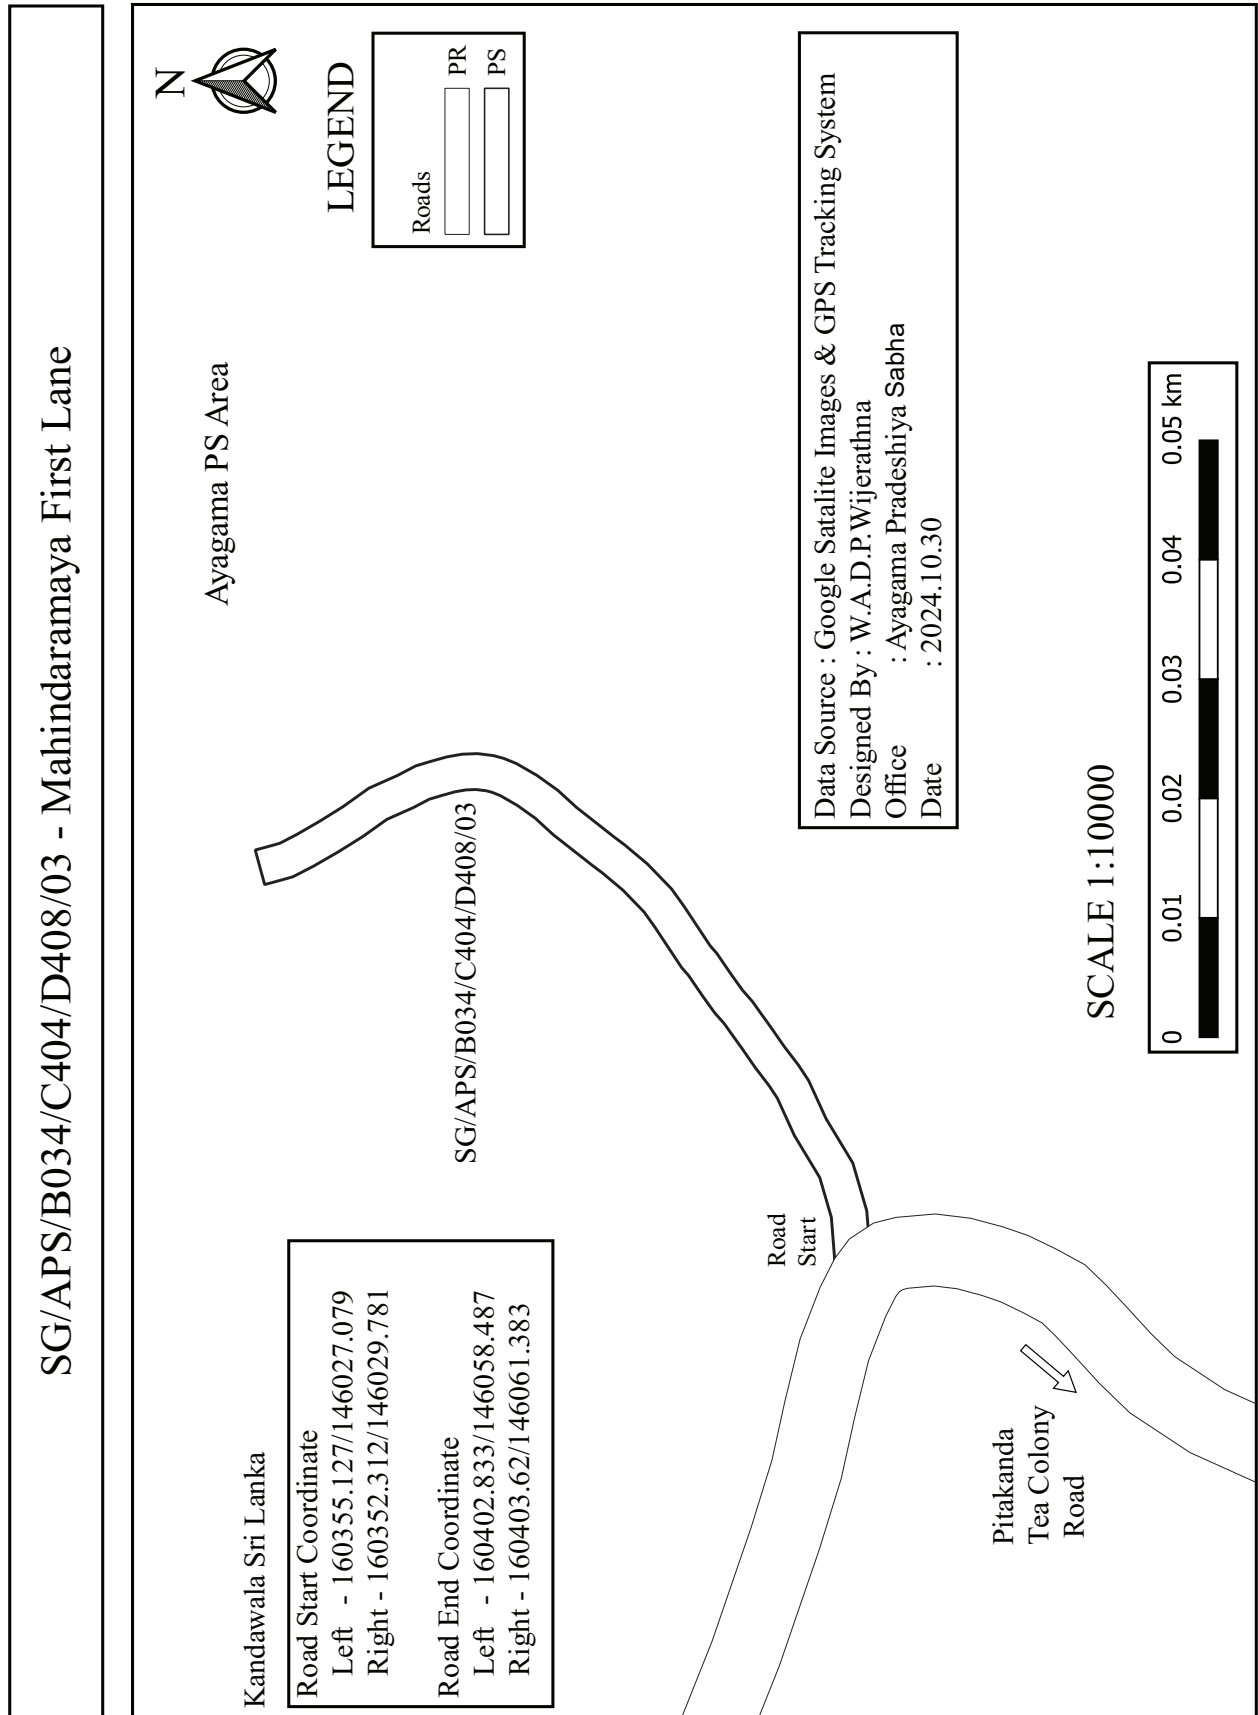

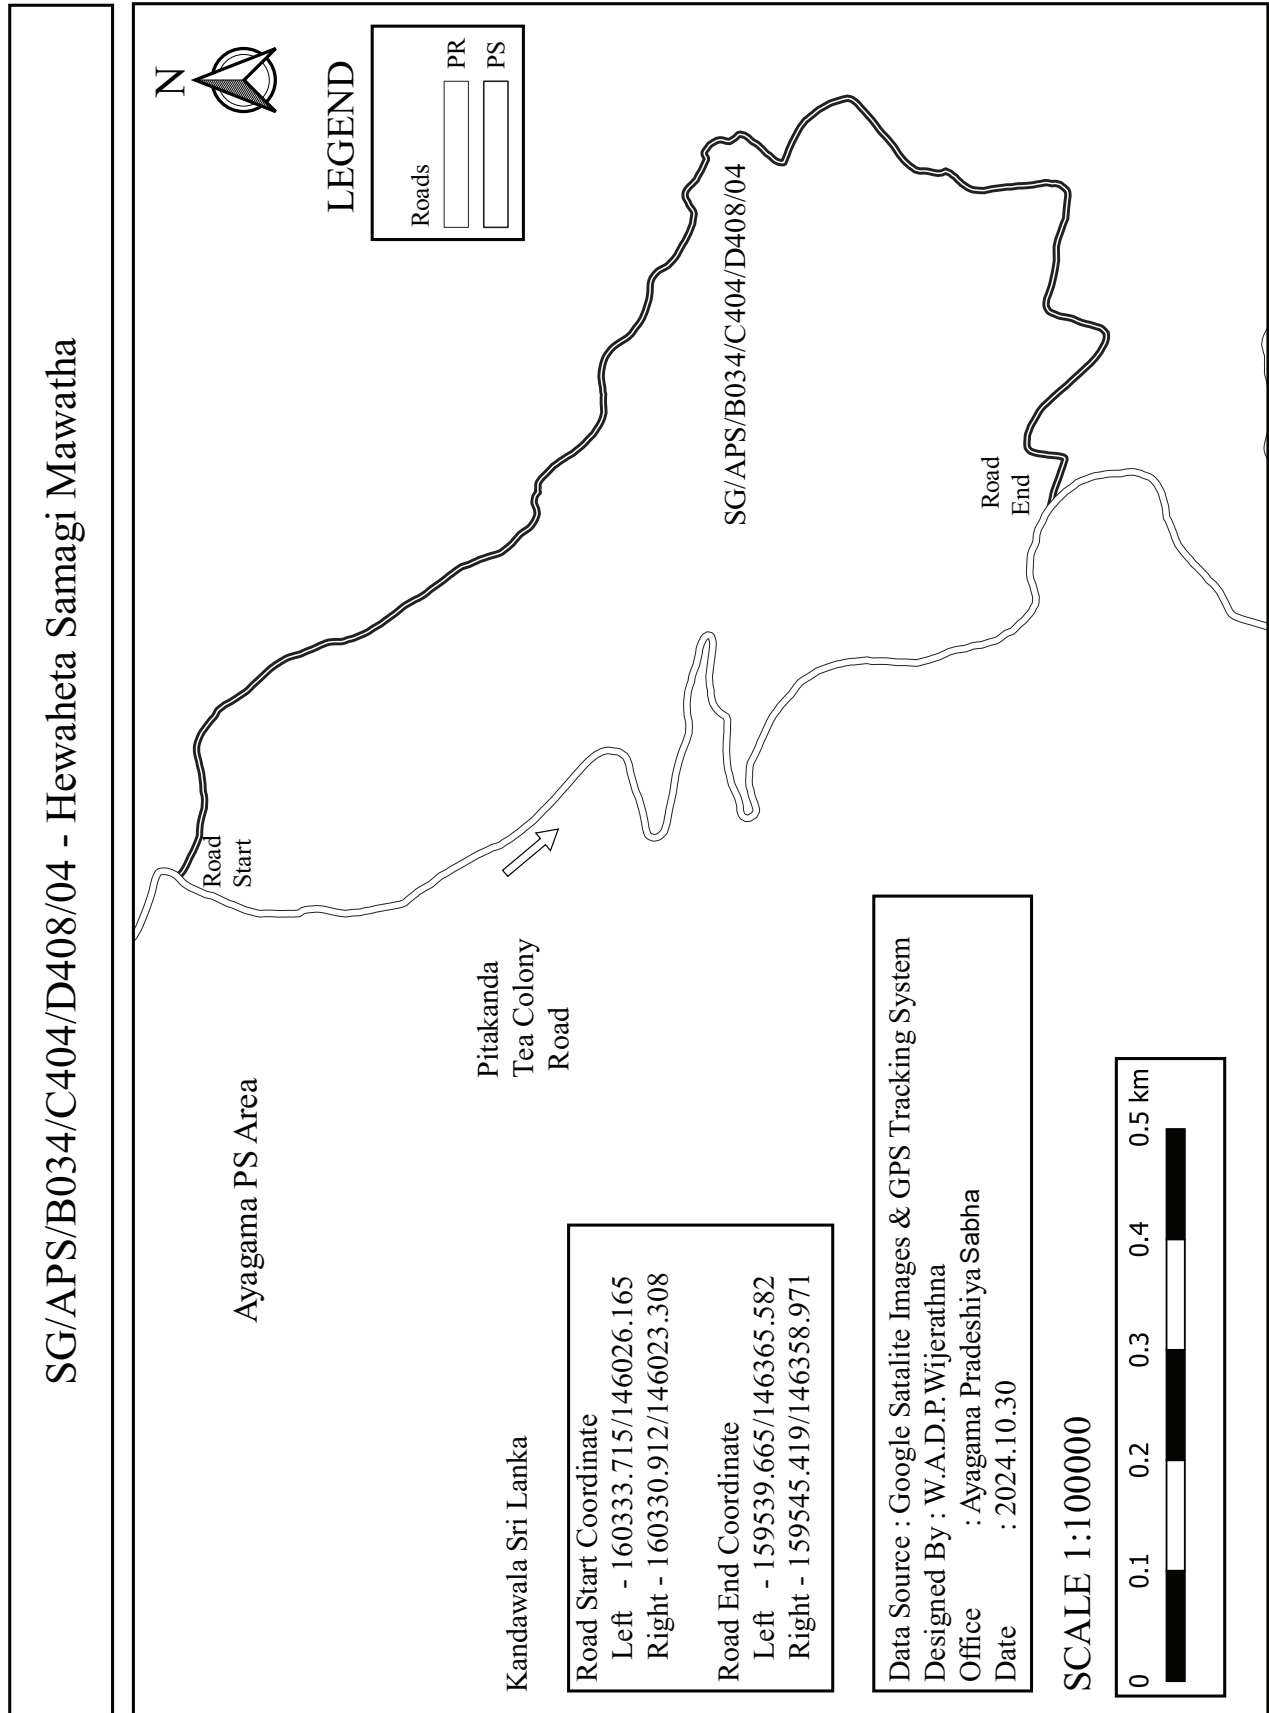

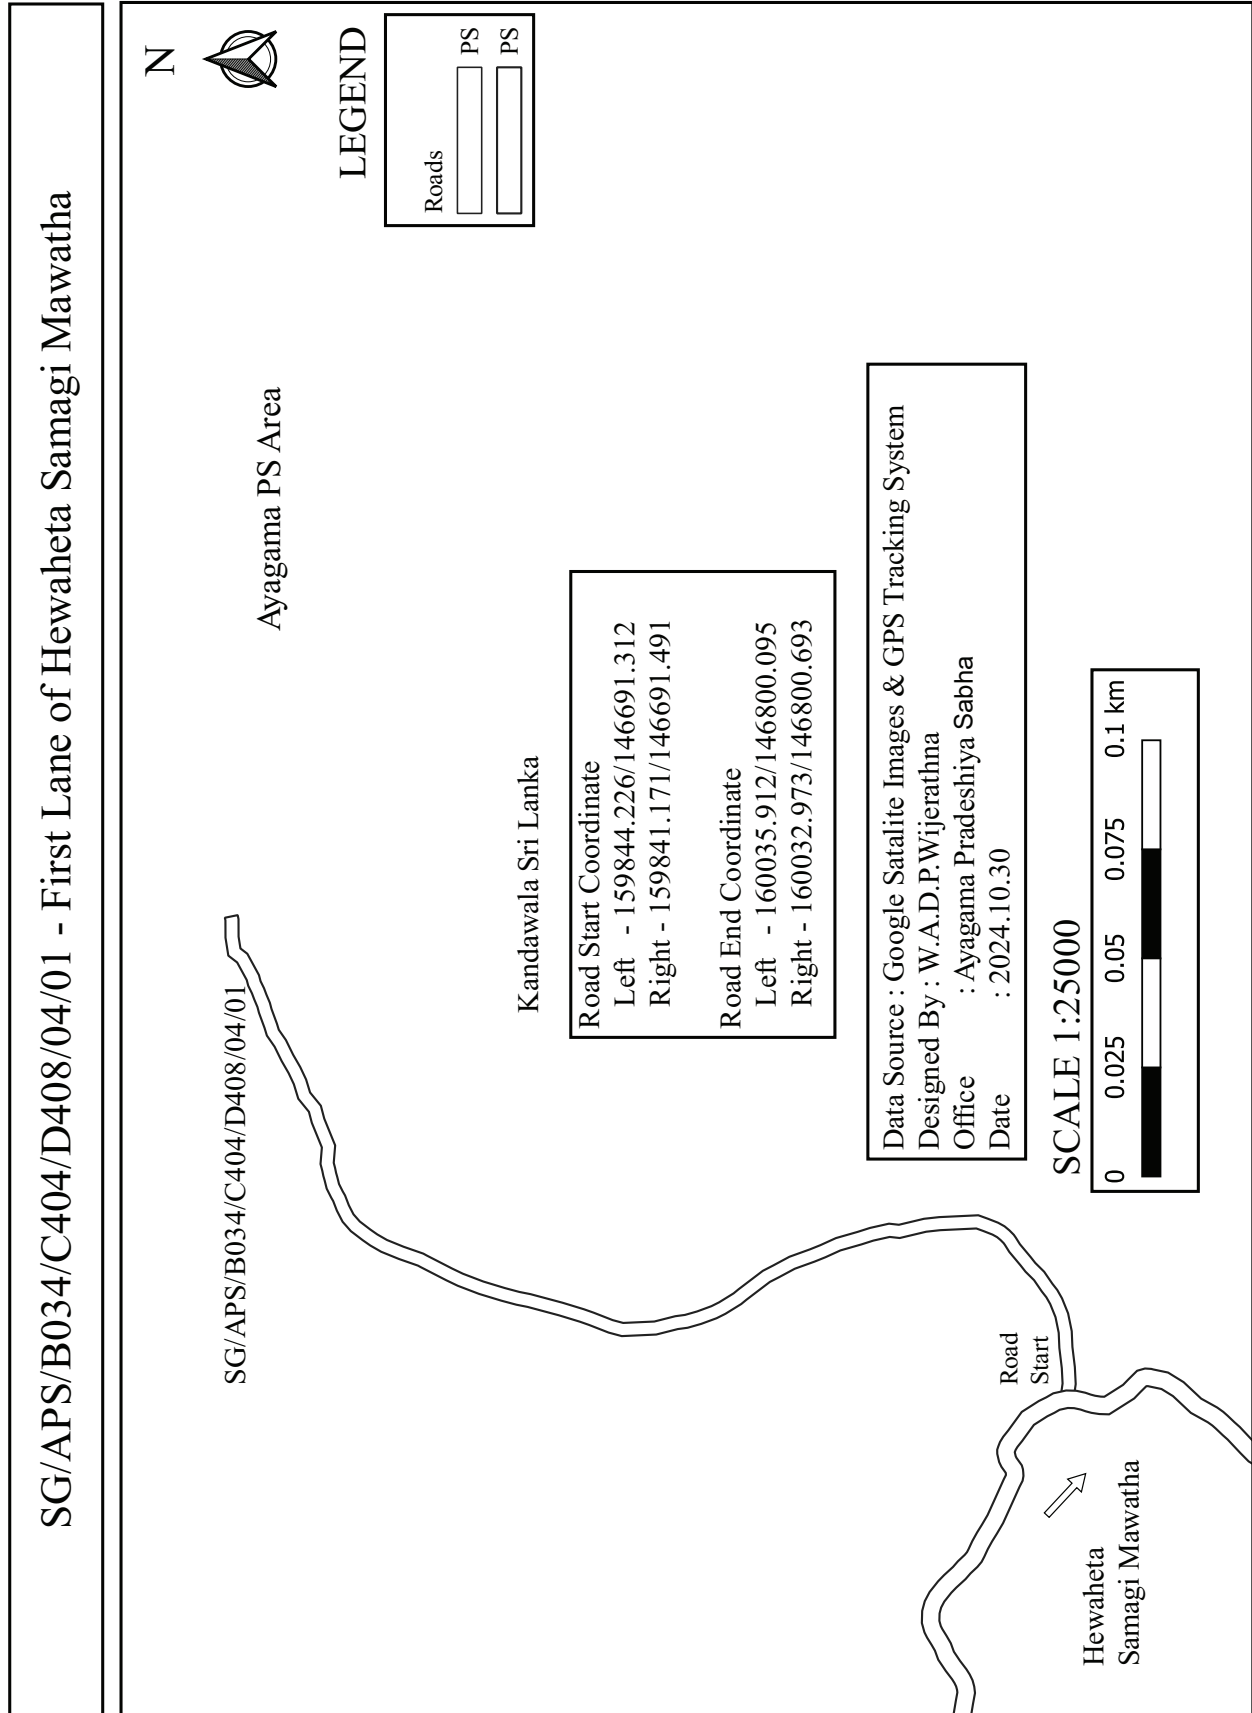


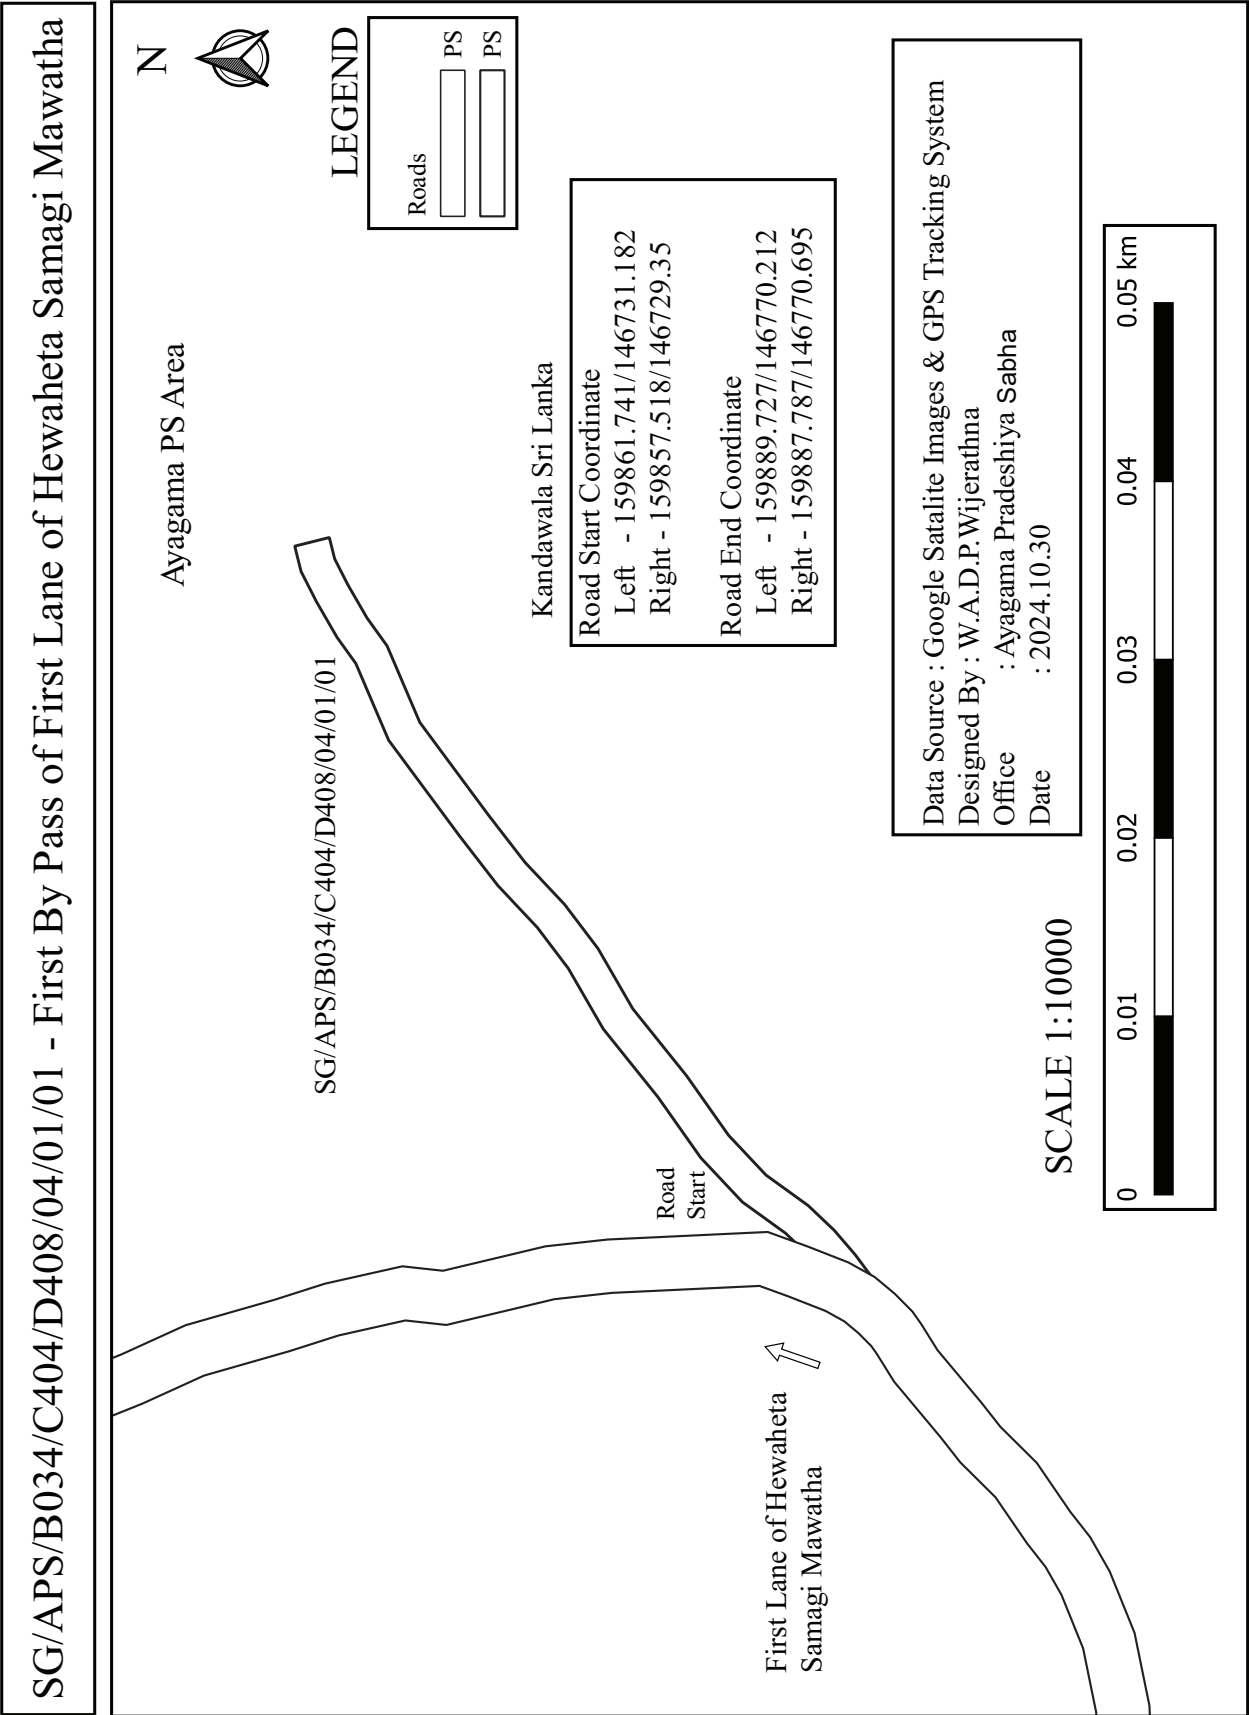


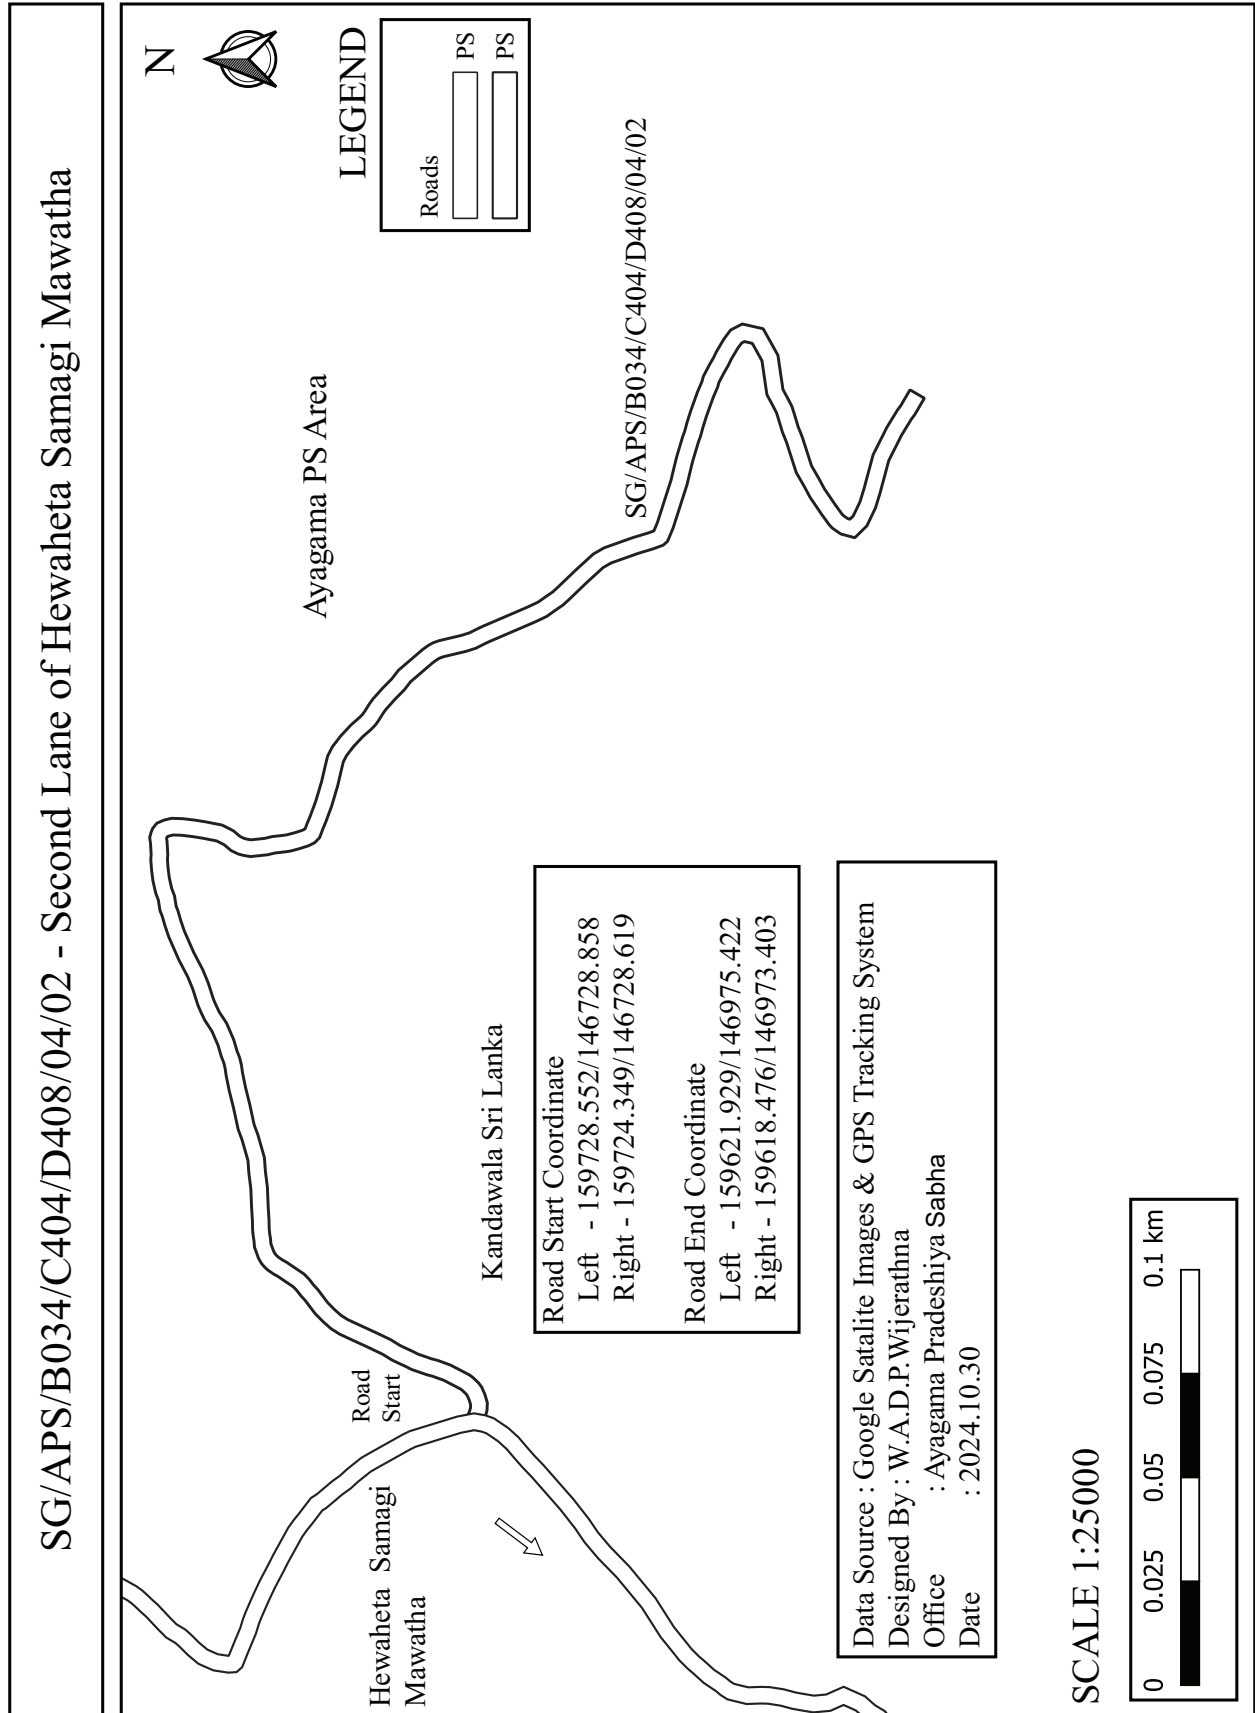



SG/APS/B034/C404/D408/04/02/01 - Footpath - First By Pass Way of Second Lane of Hewaheta


Samagi Mawatha

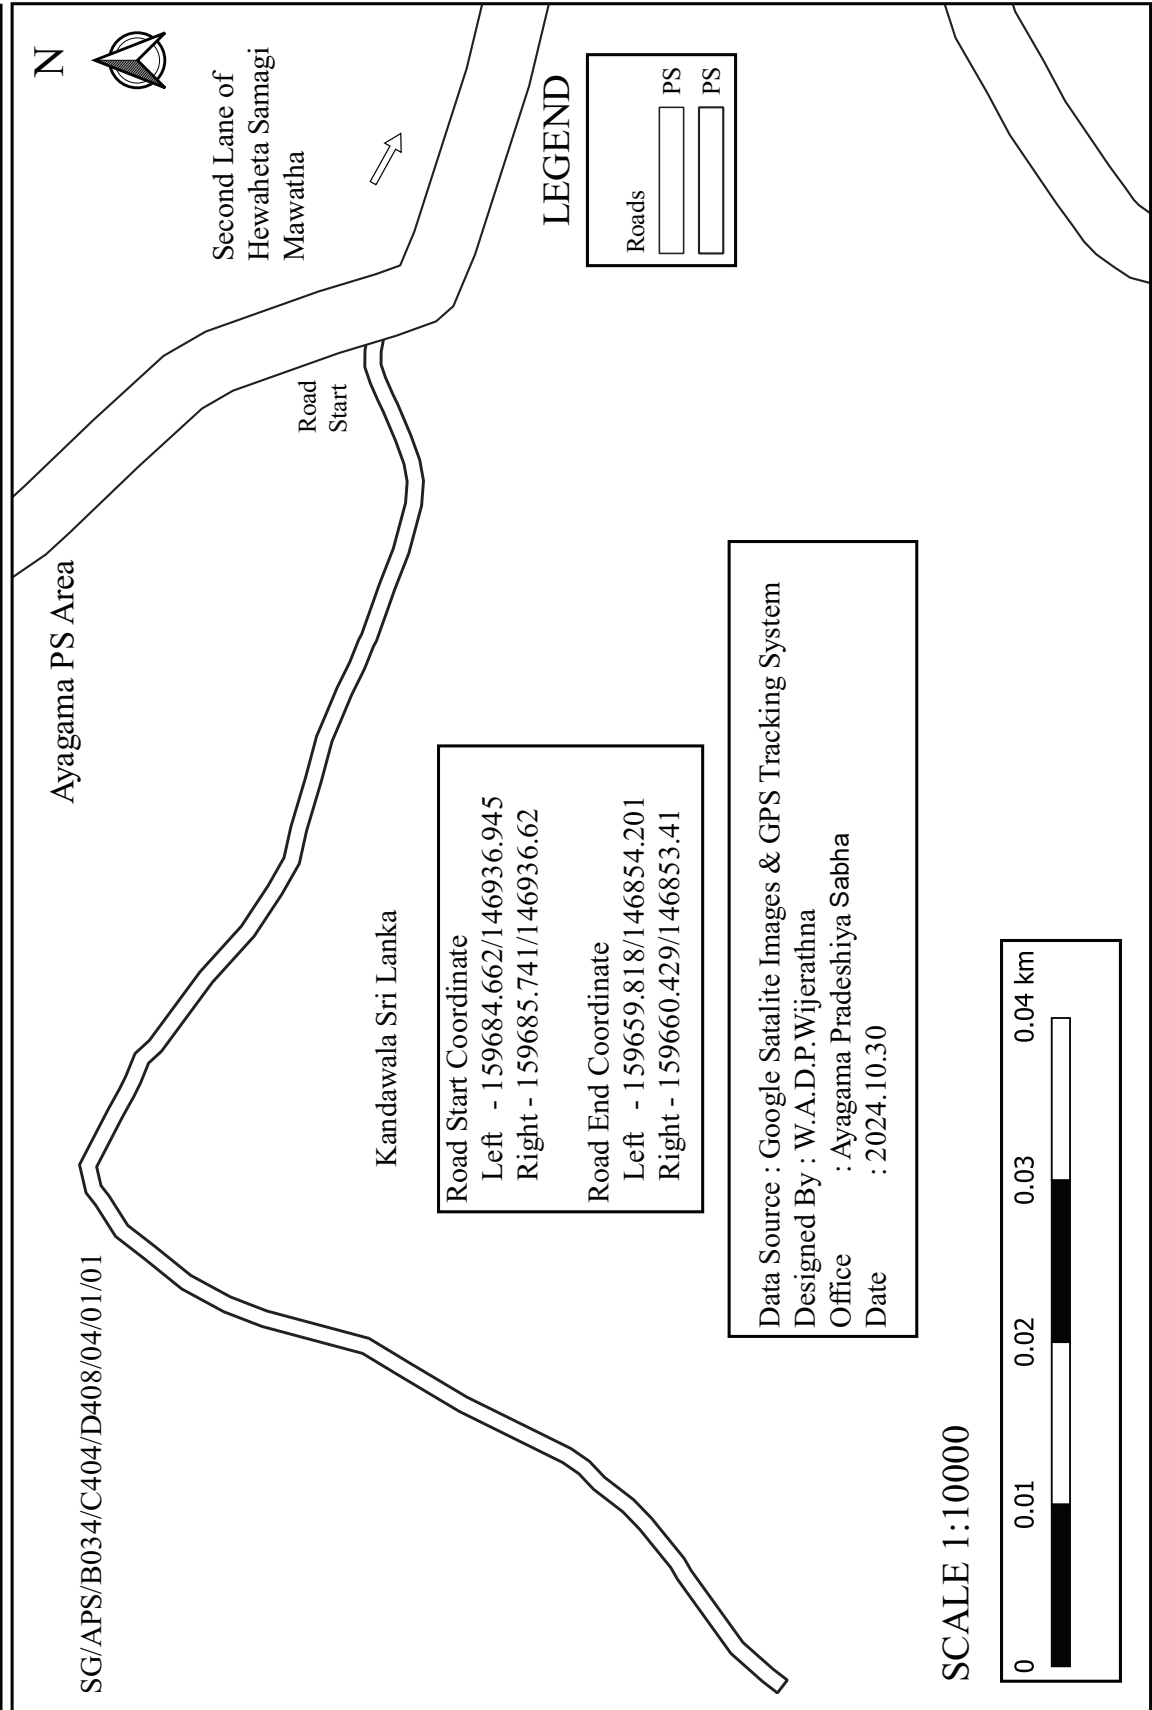


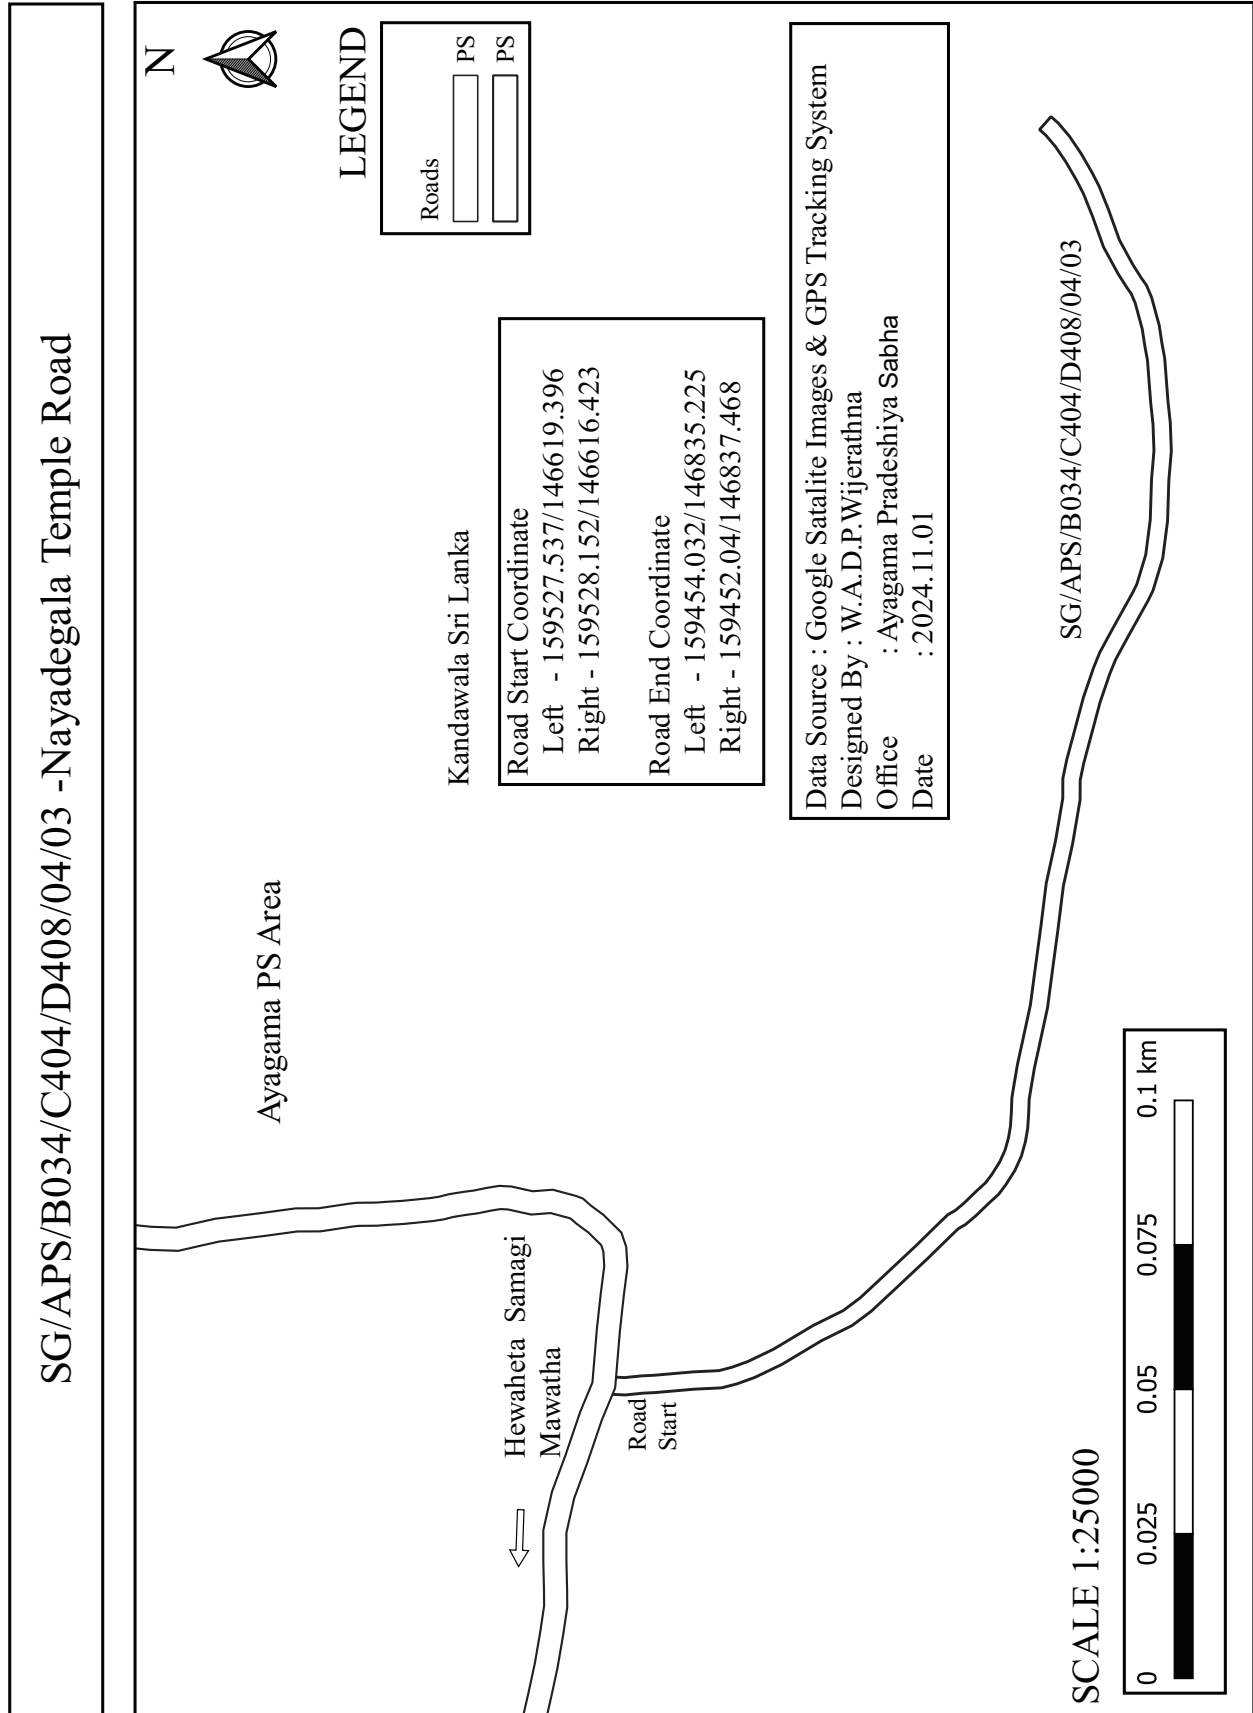

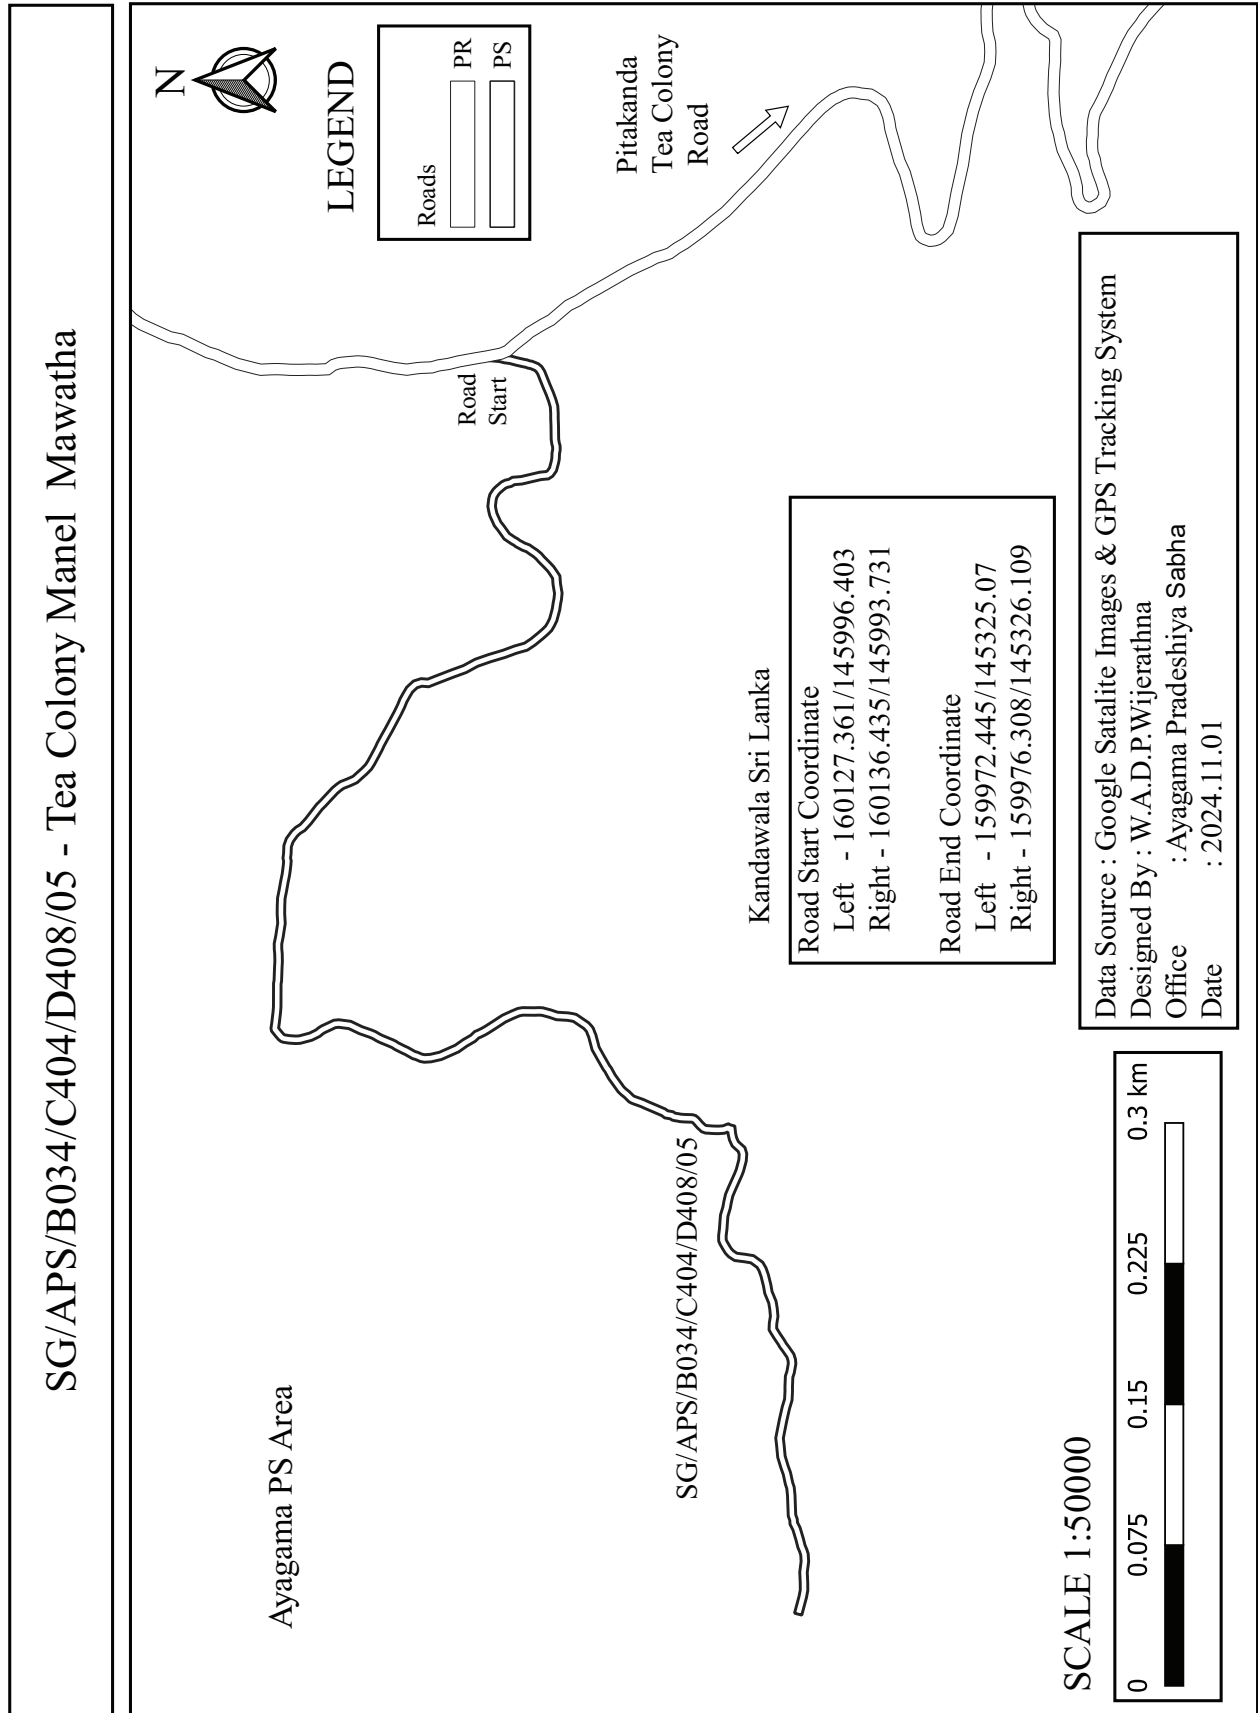

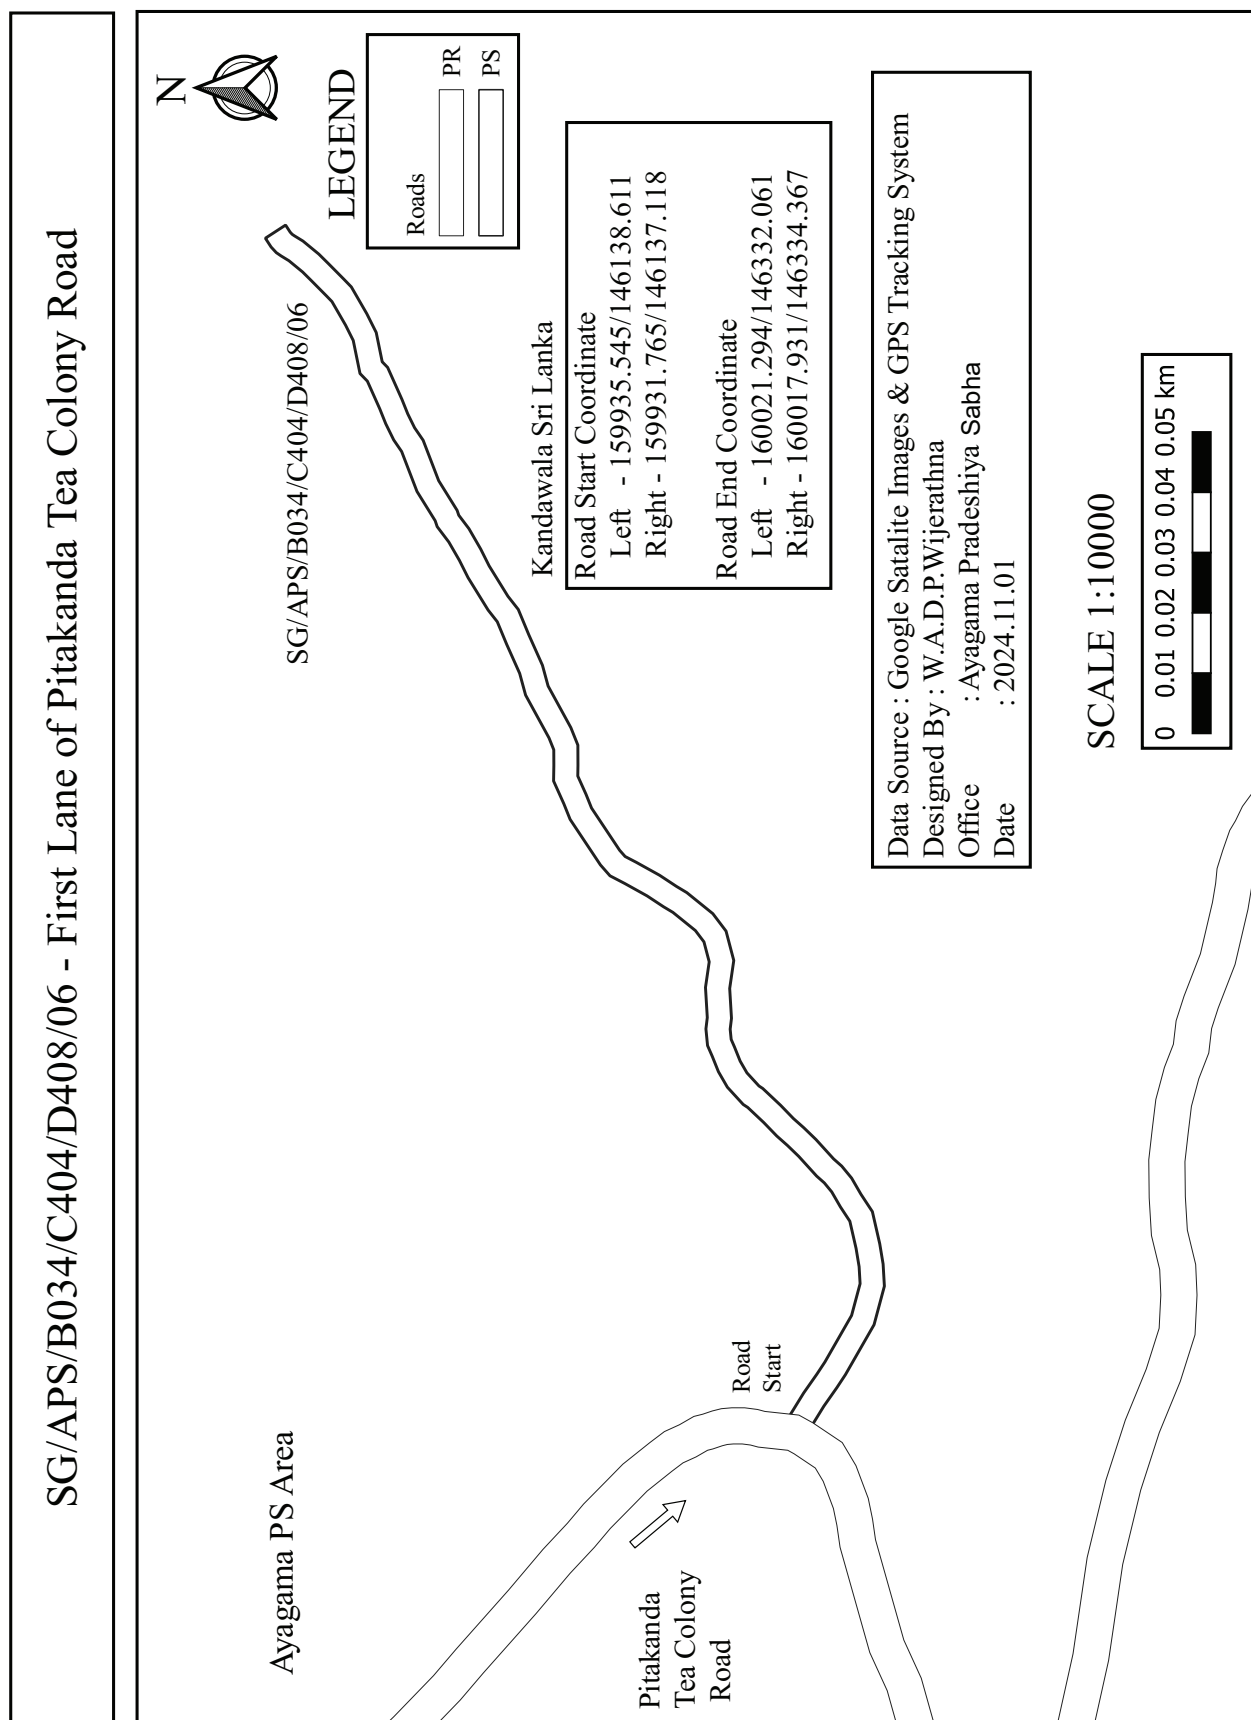


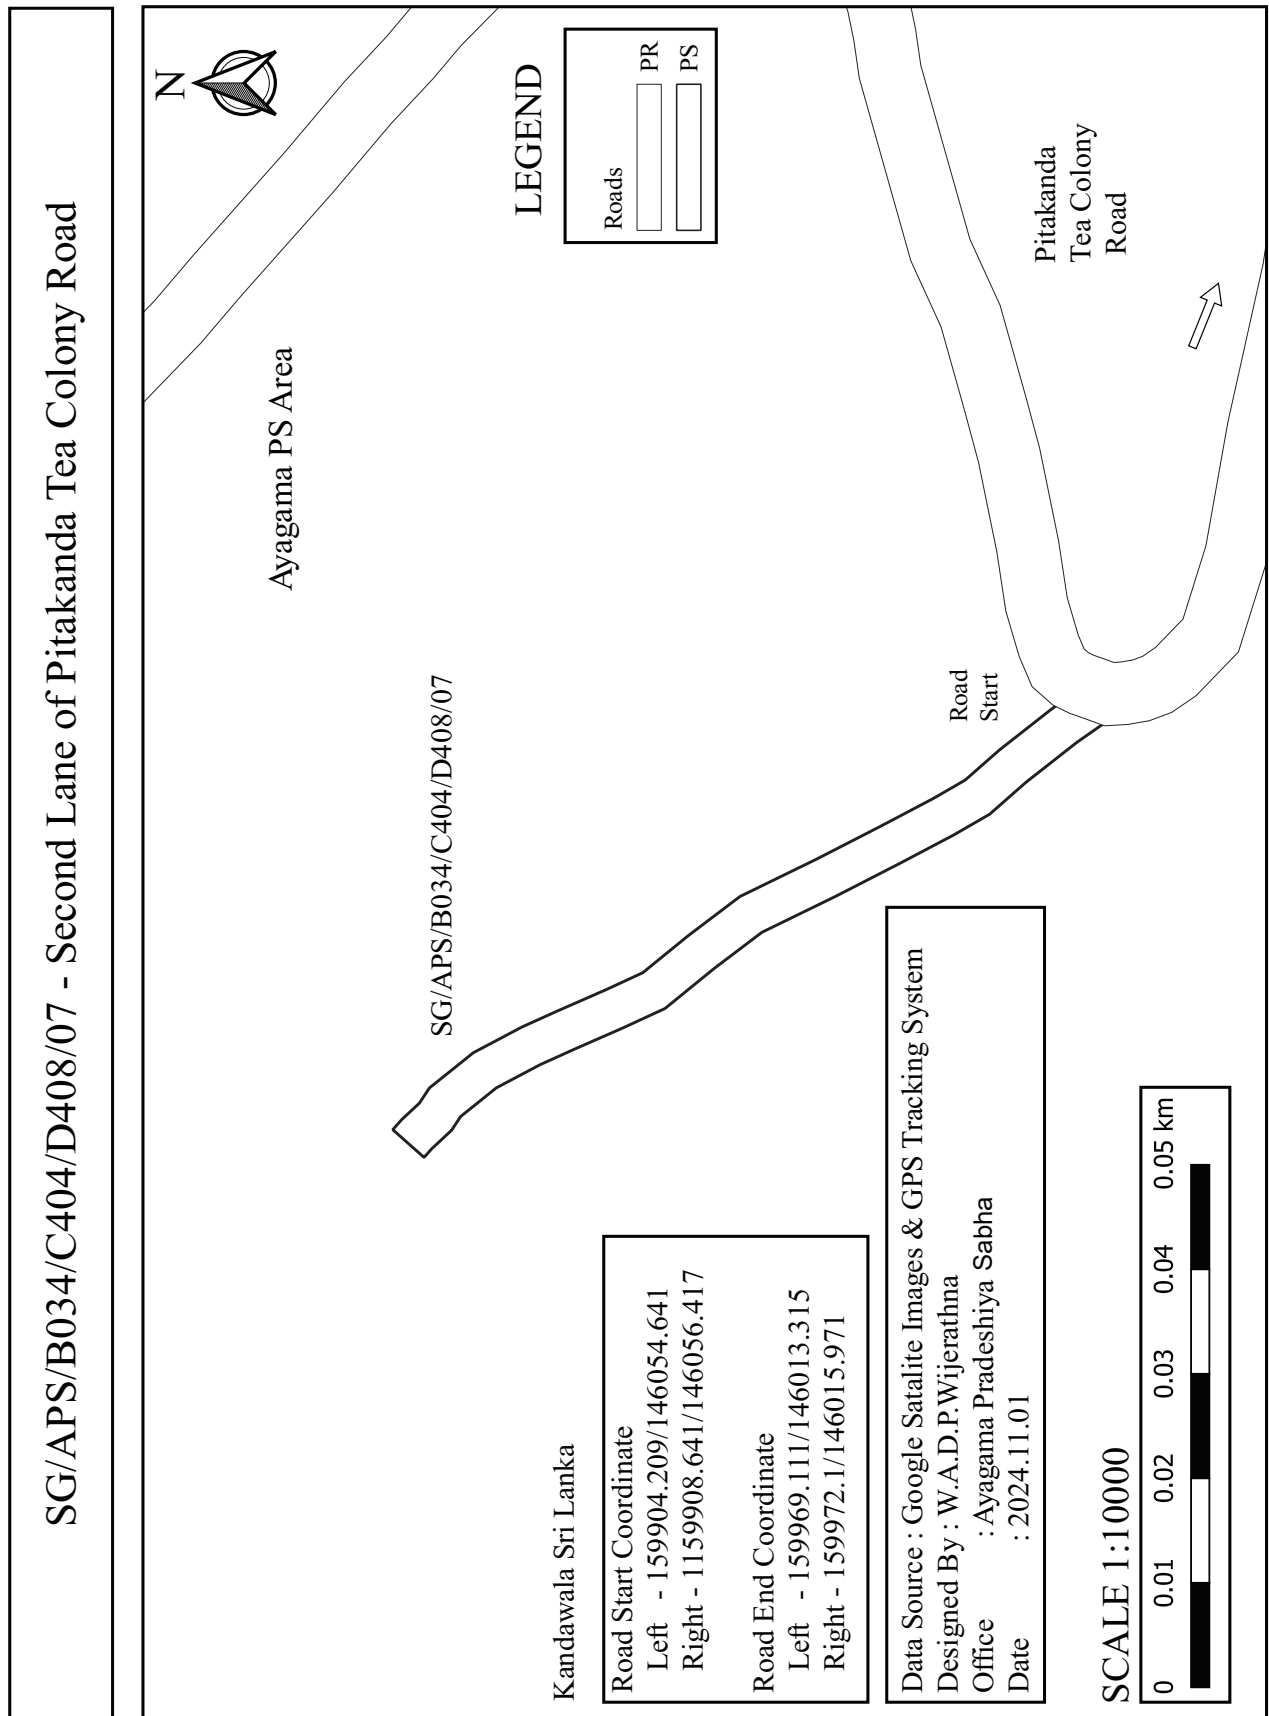


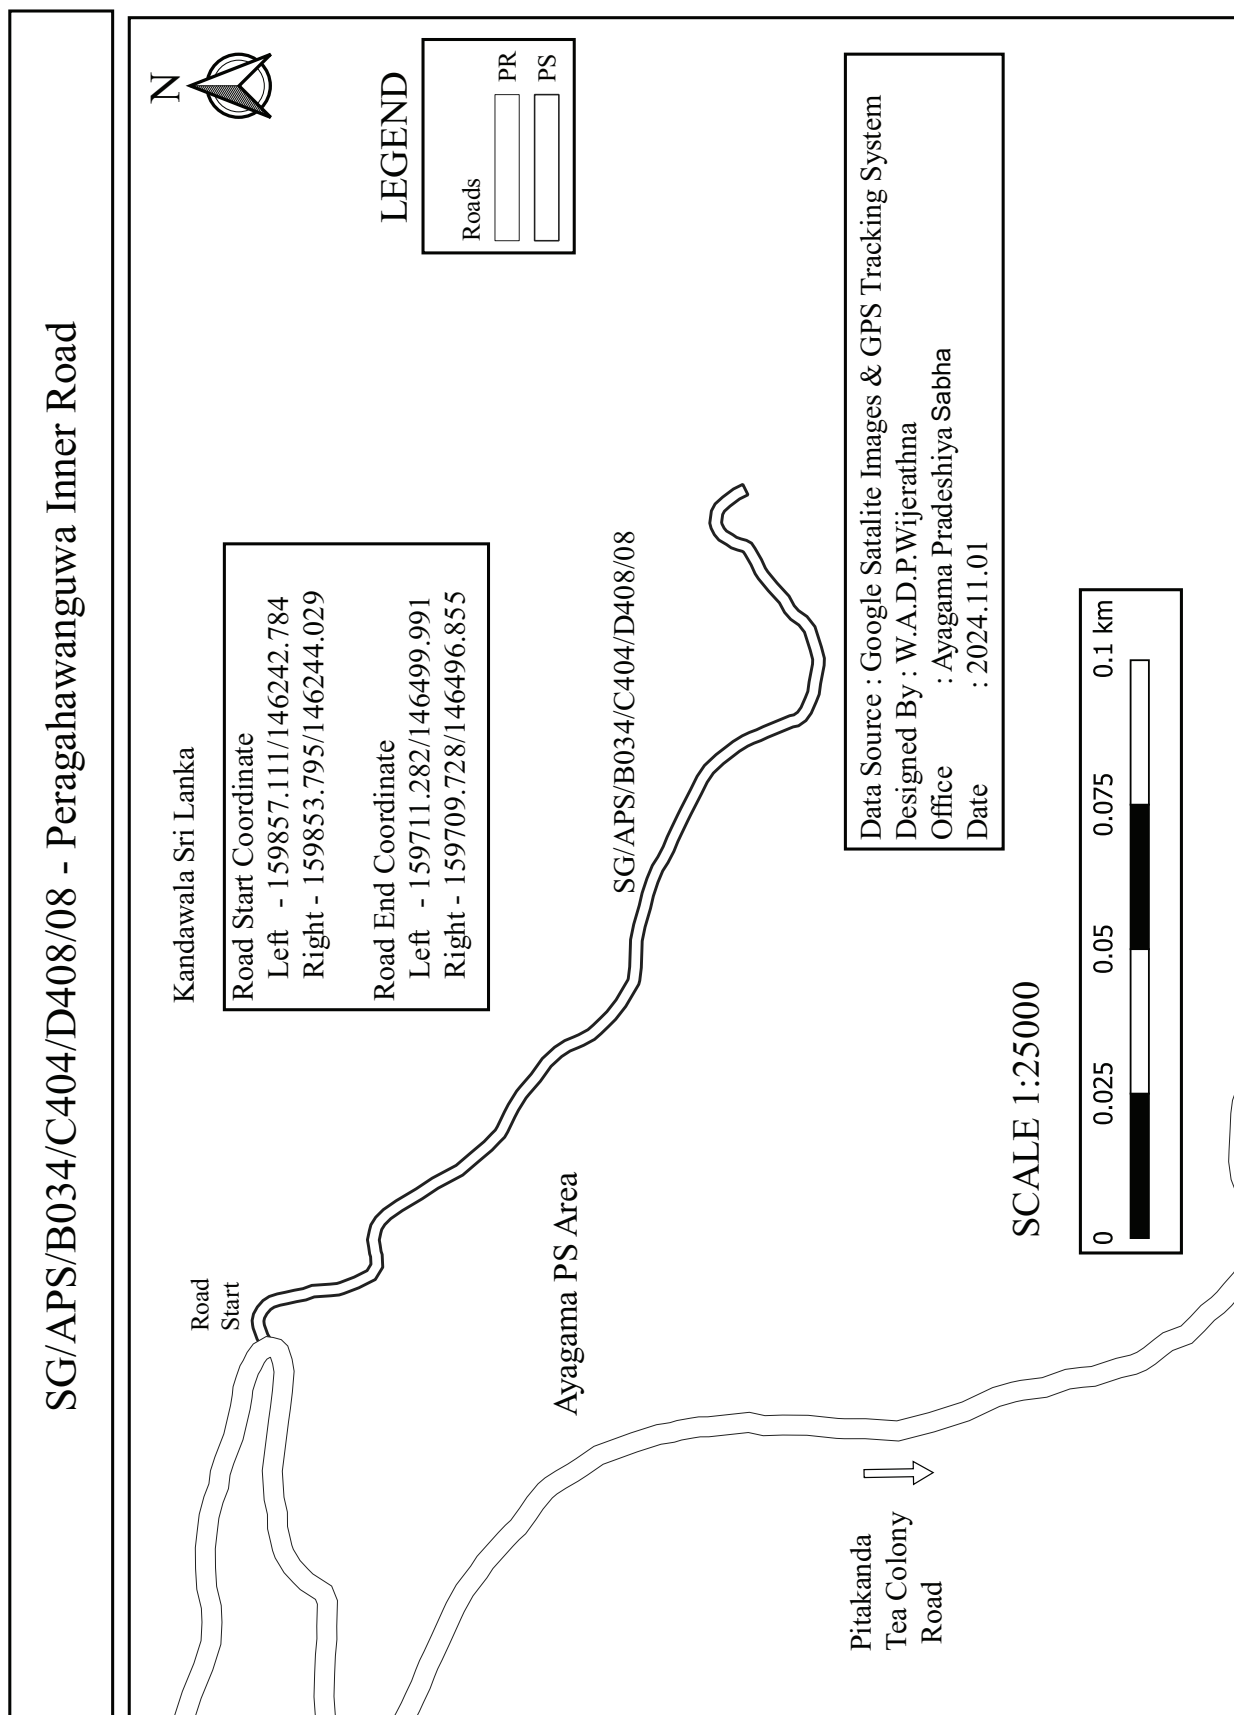





SG/APS/B034/C404/D408/10 - Tea Colony Batahena Road

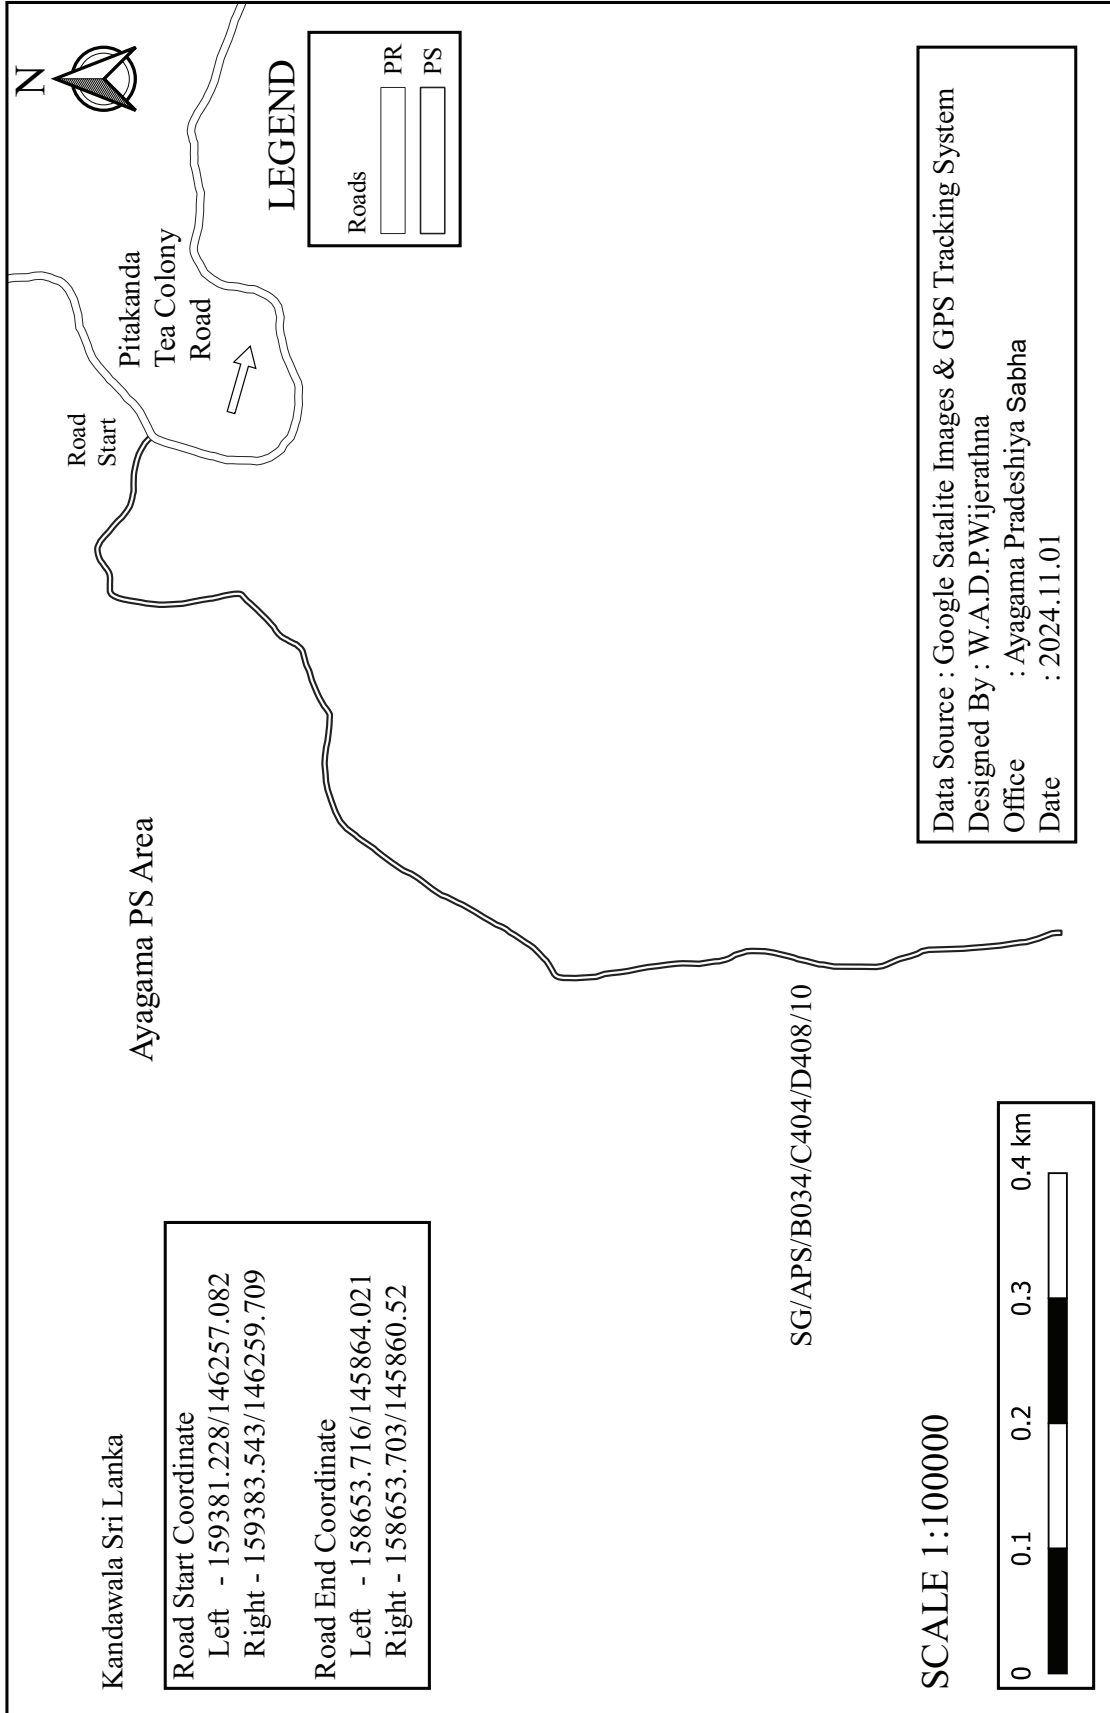

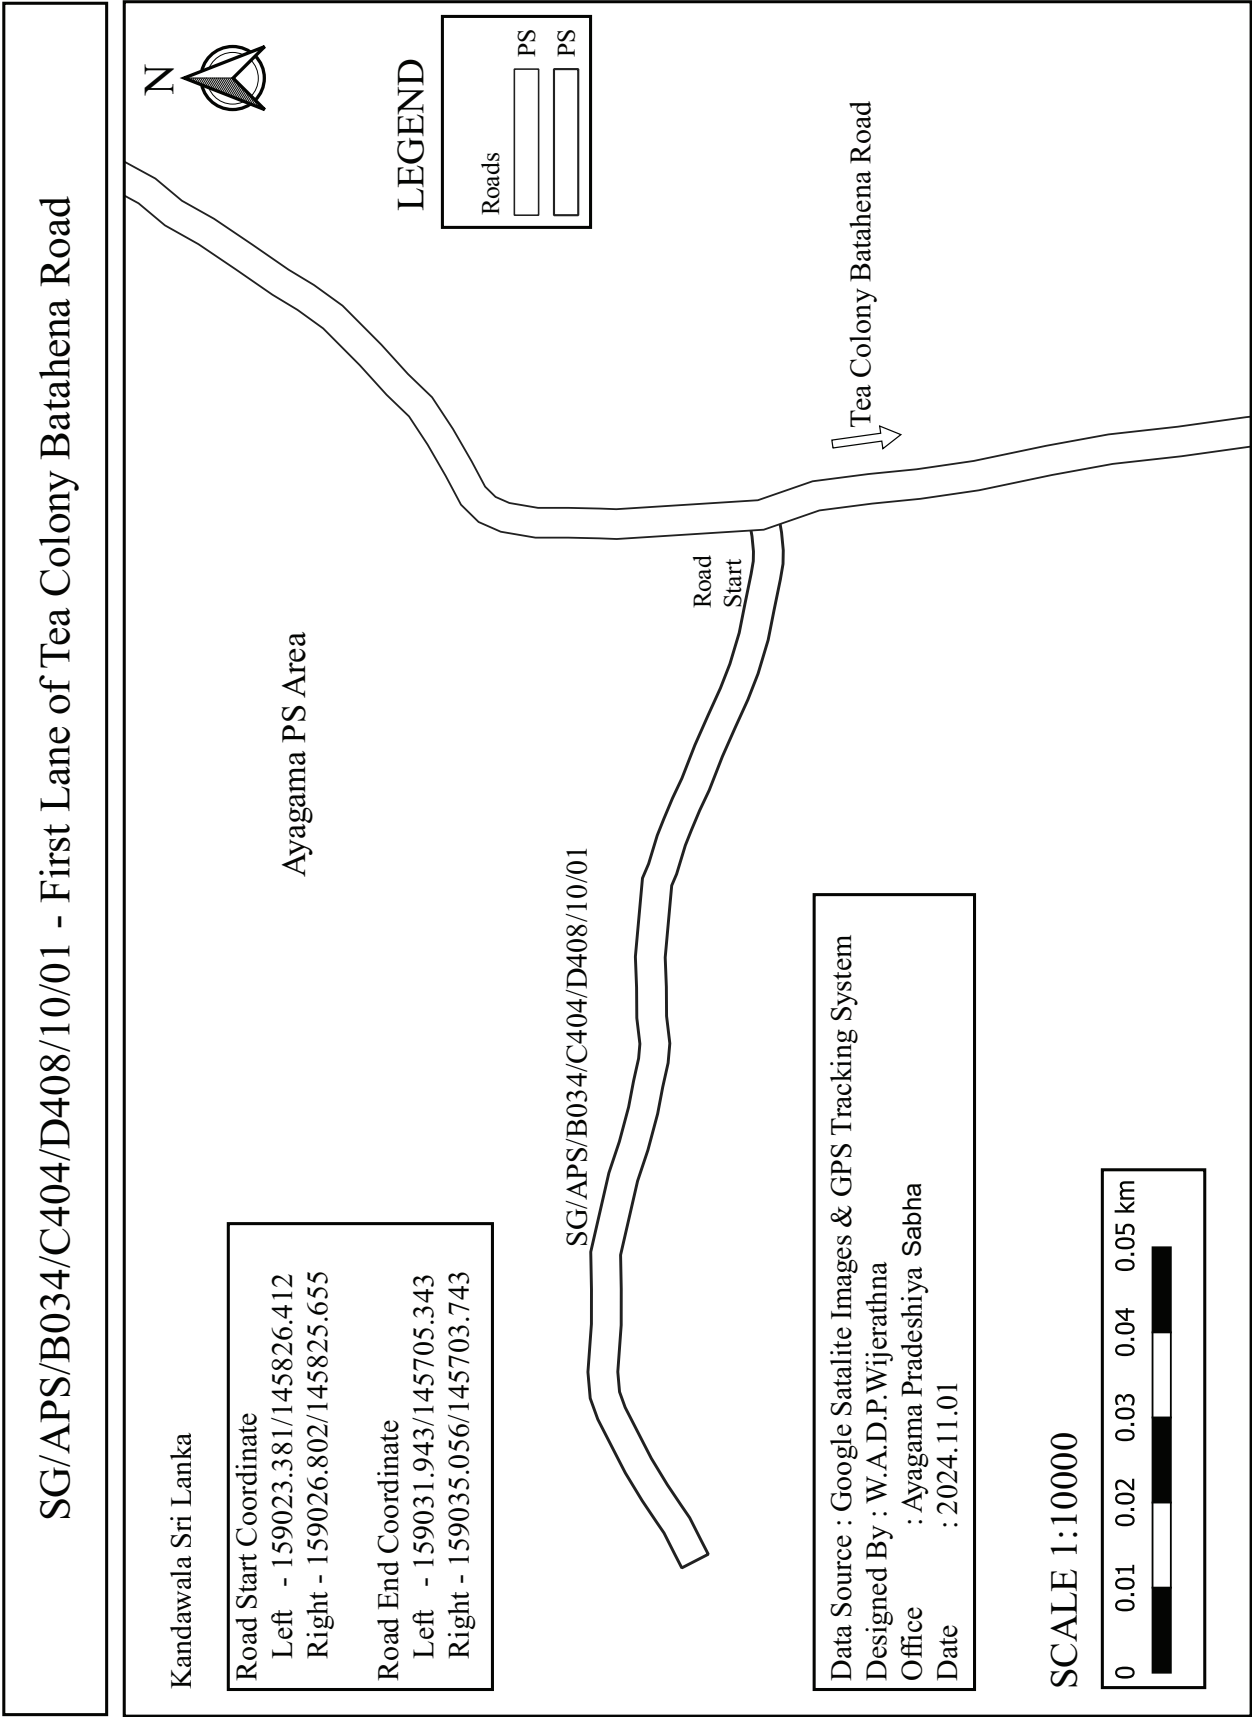



SG/APS/B034/C404/D408/10/02 - Batahena Gangabadathenna Road

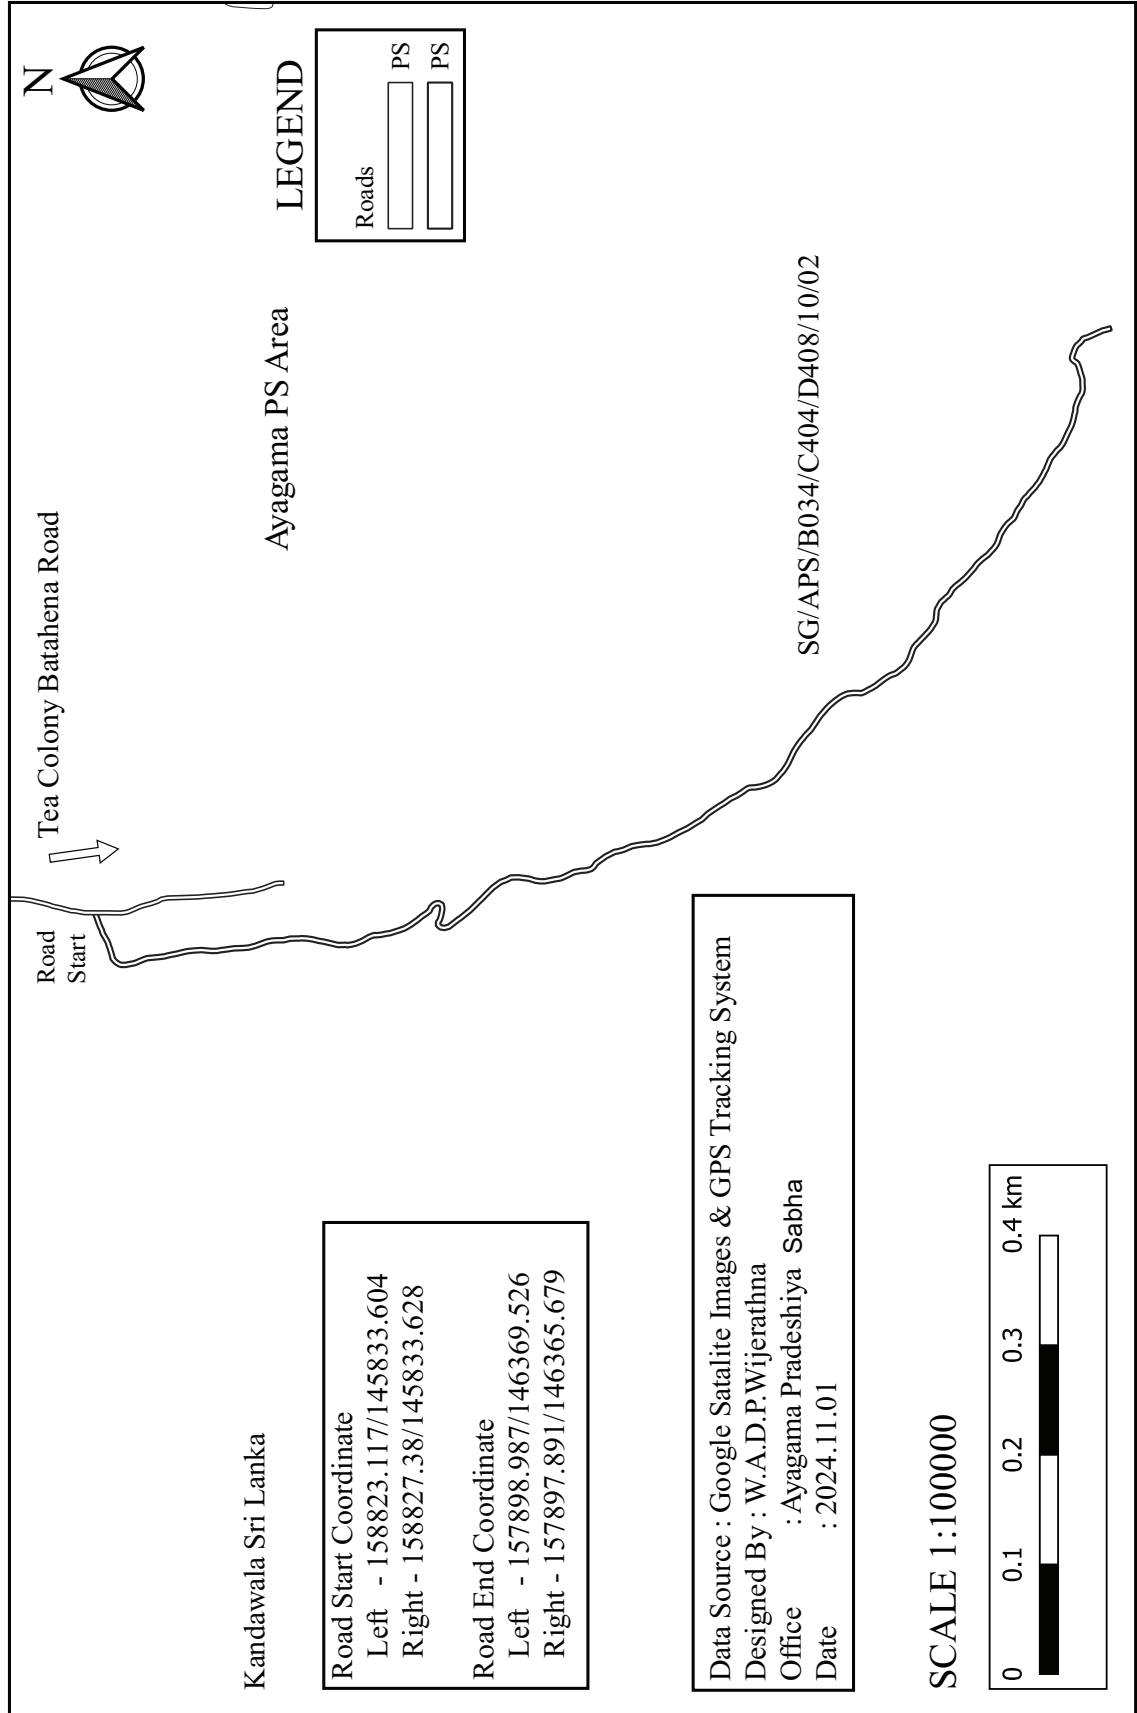

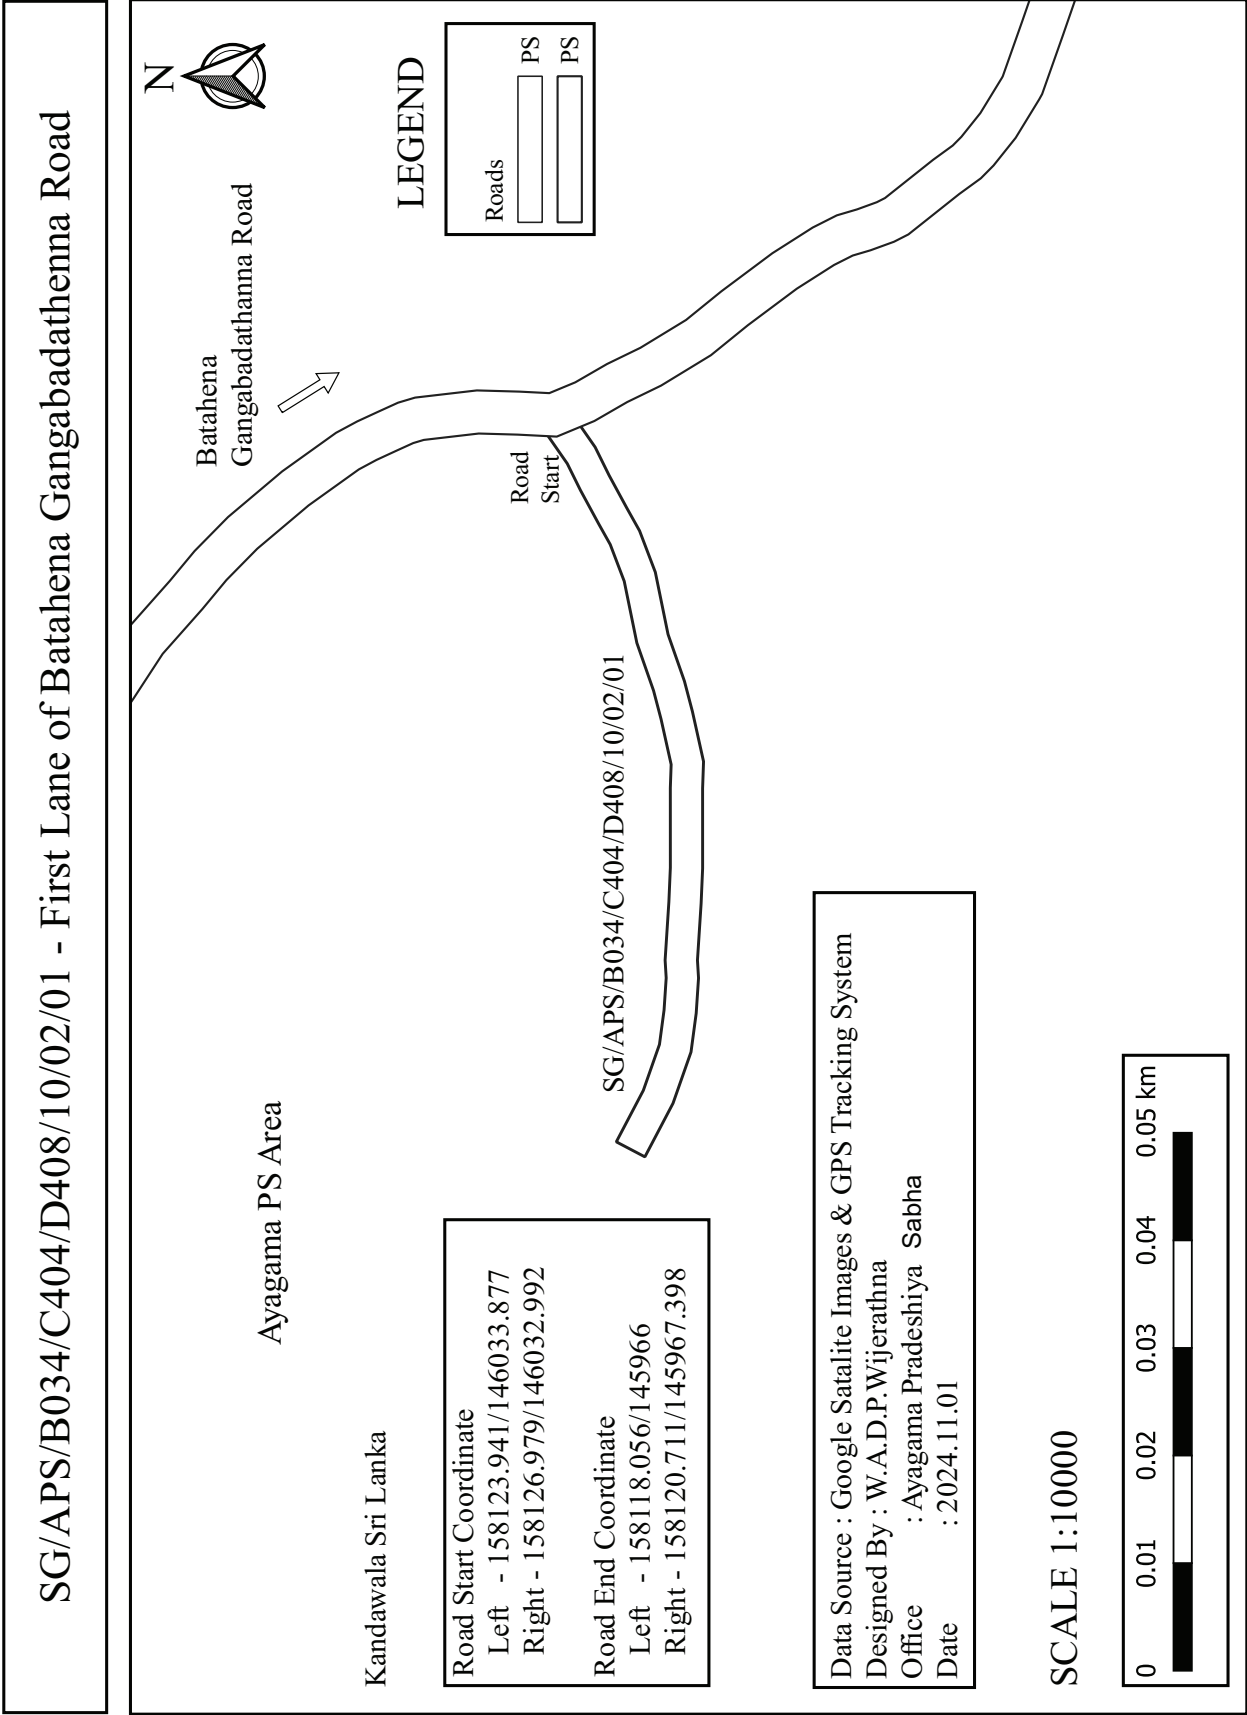



SG/APS/B034/C404/D408/10/03 - Batahena Panwilathenna Road

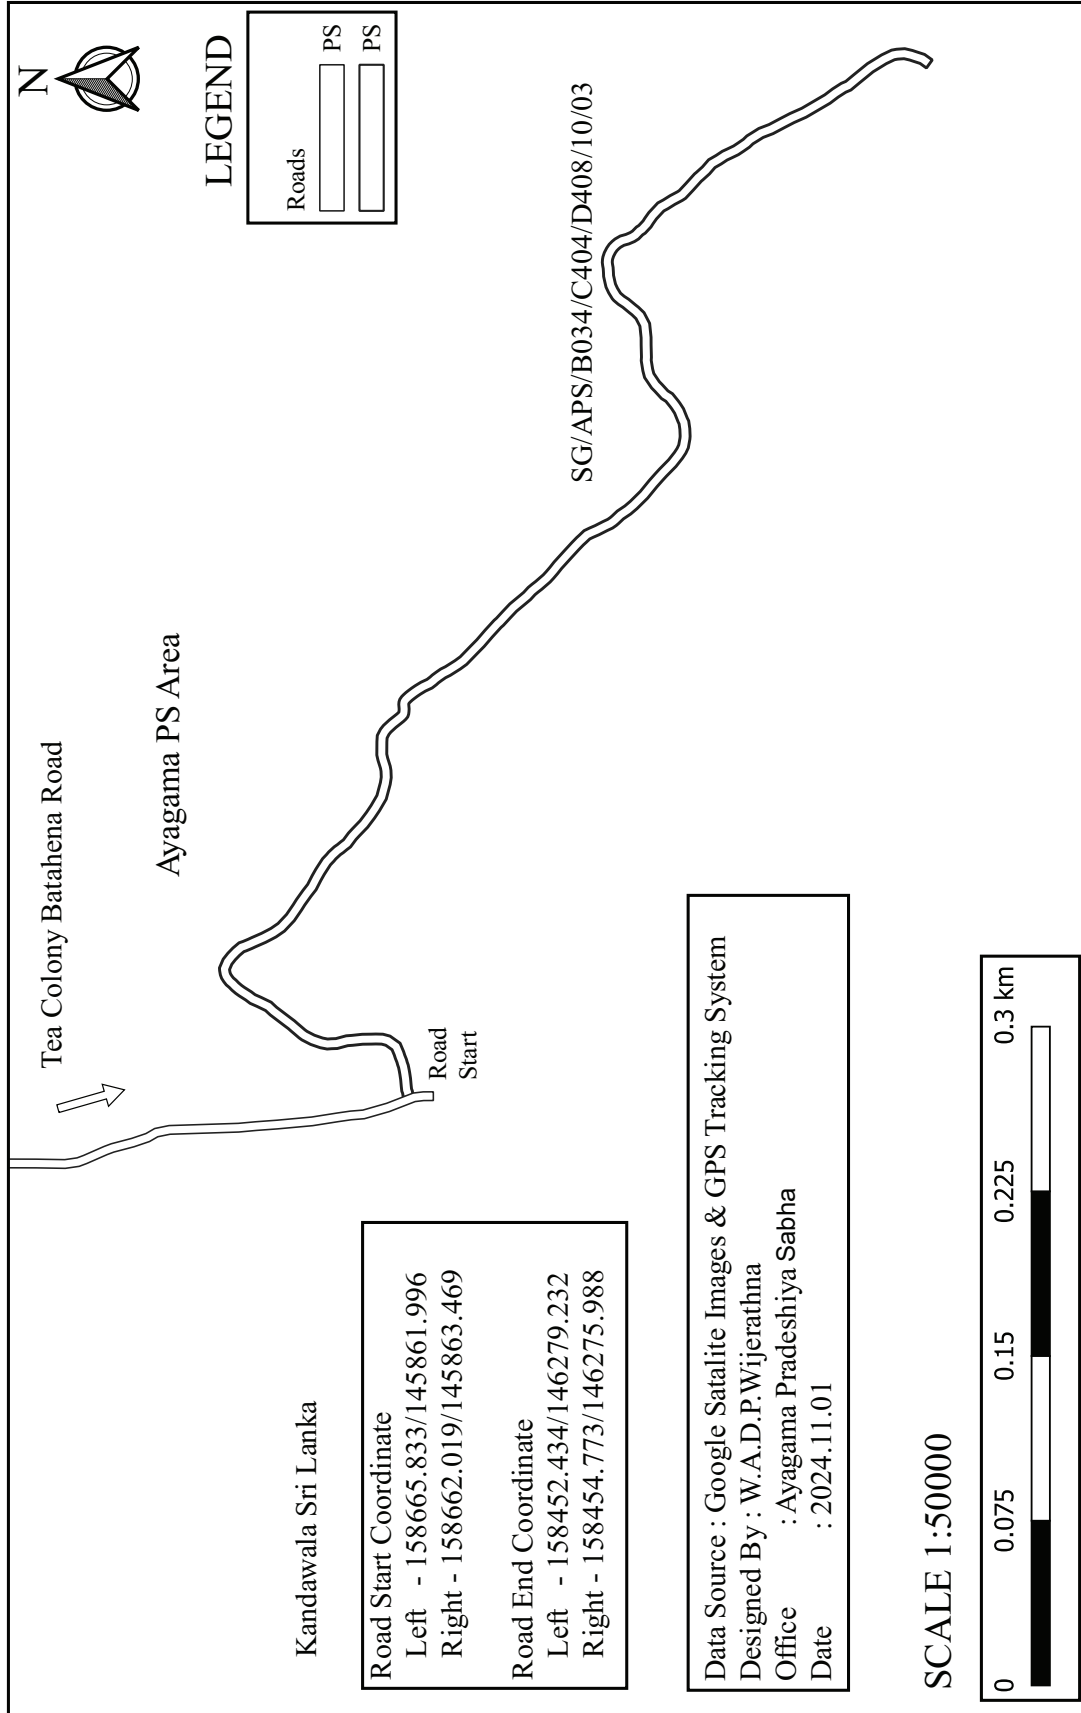


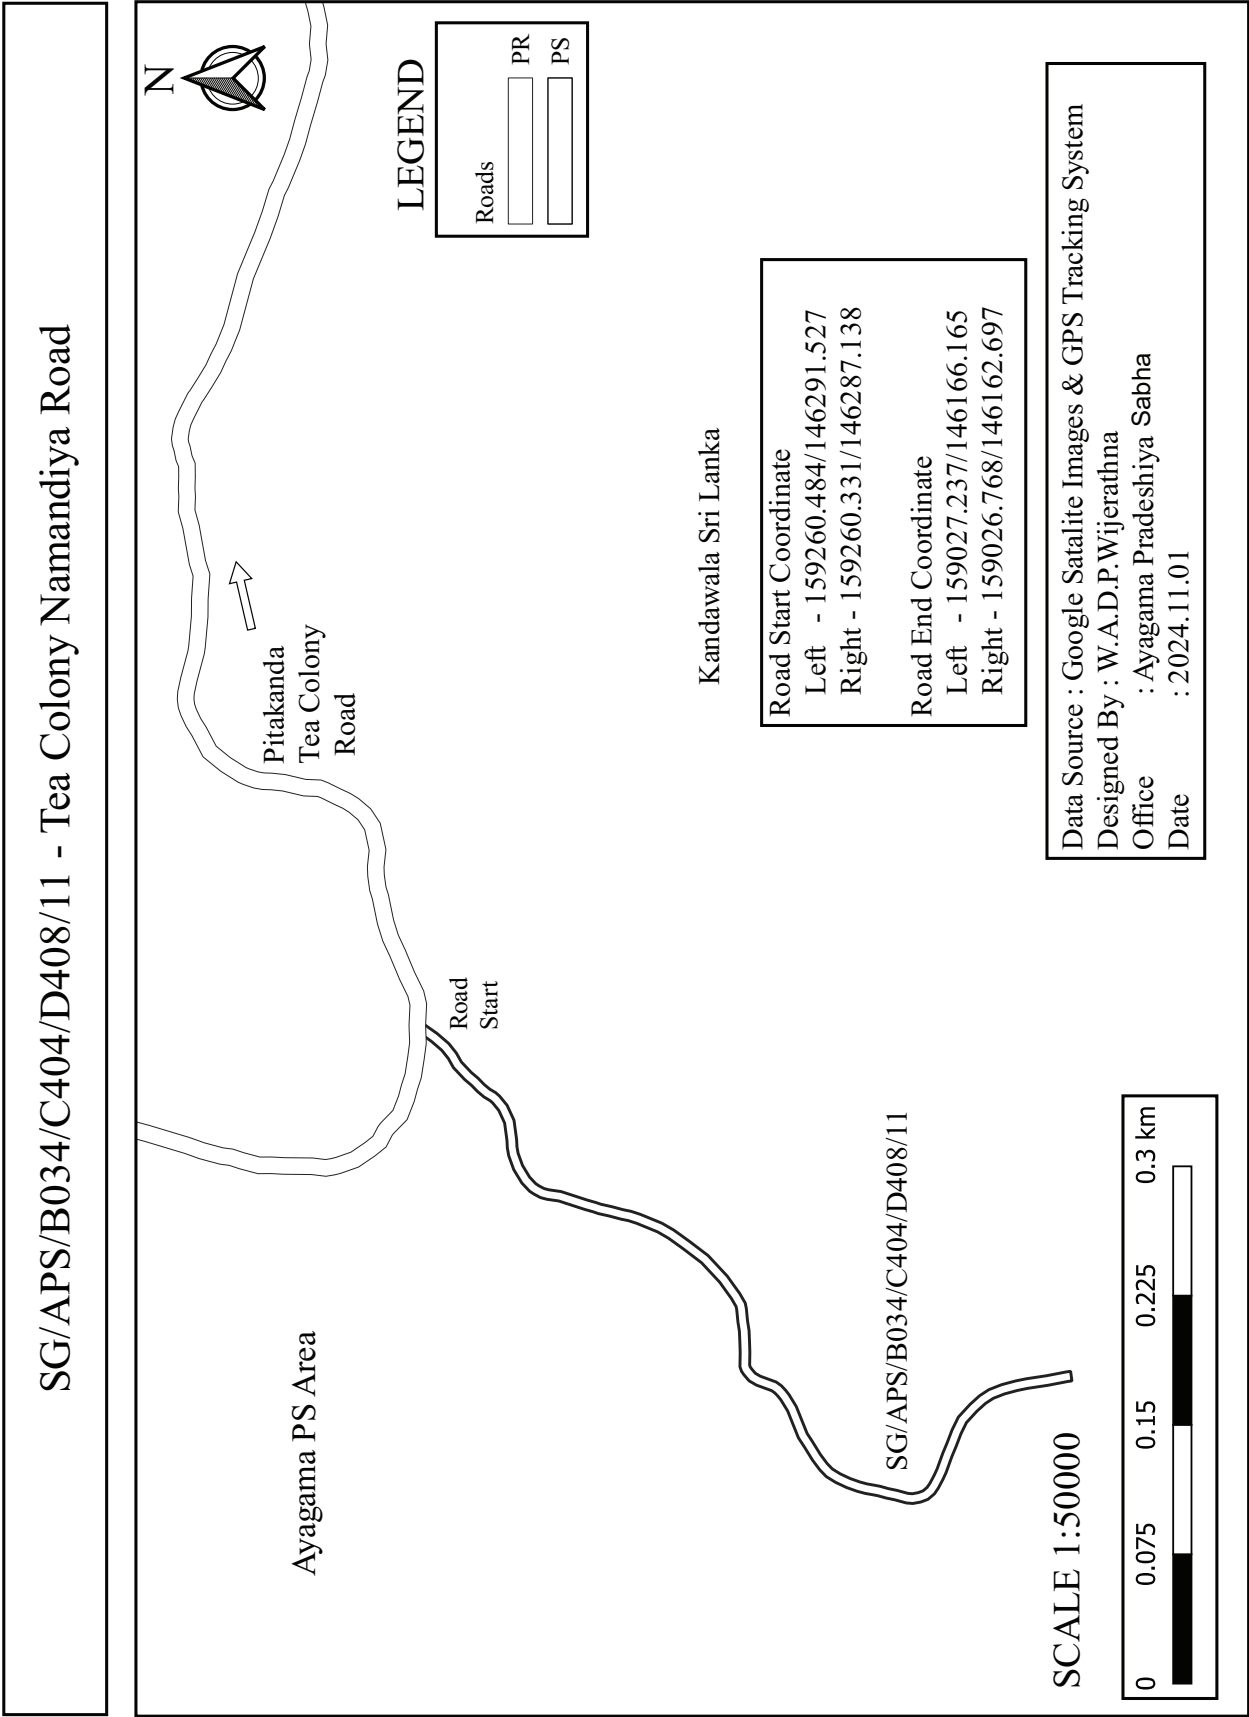


SG/APS/B034/C404/D408/12 - Kanduruwandola Galapalla Road

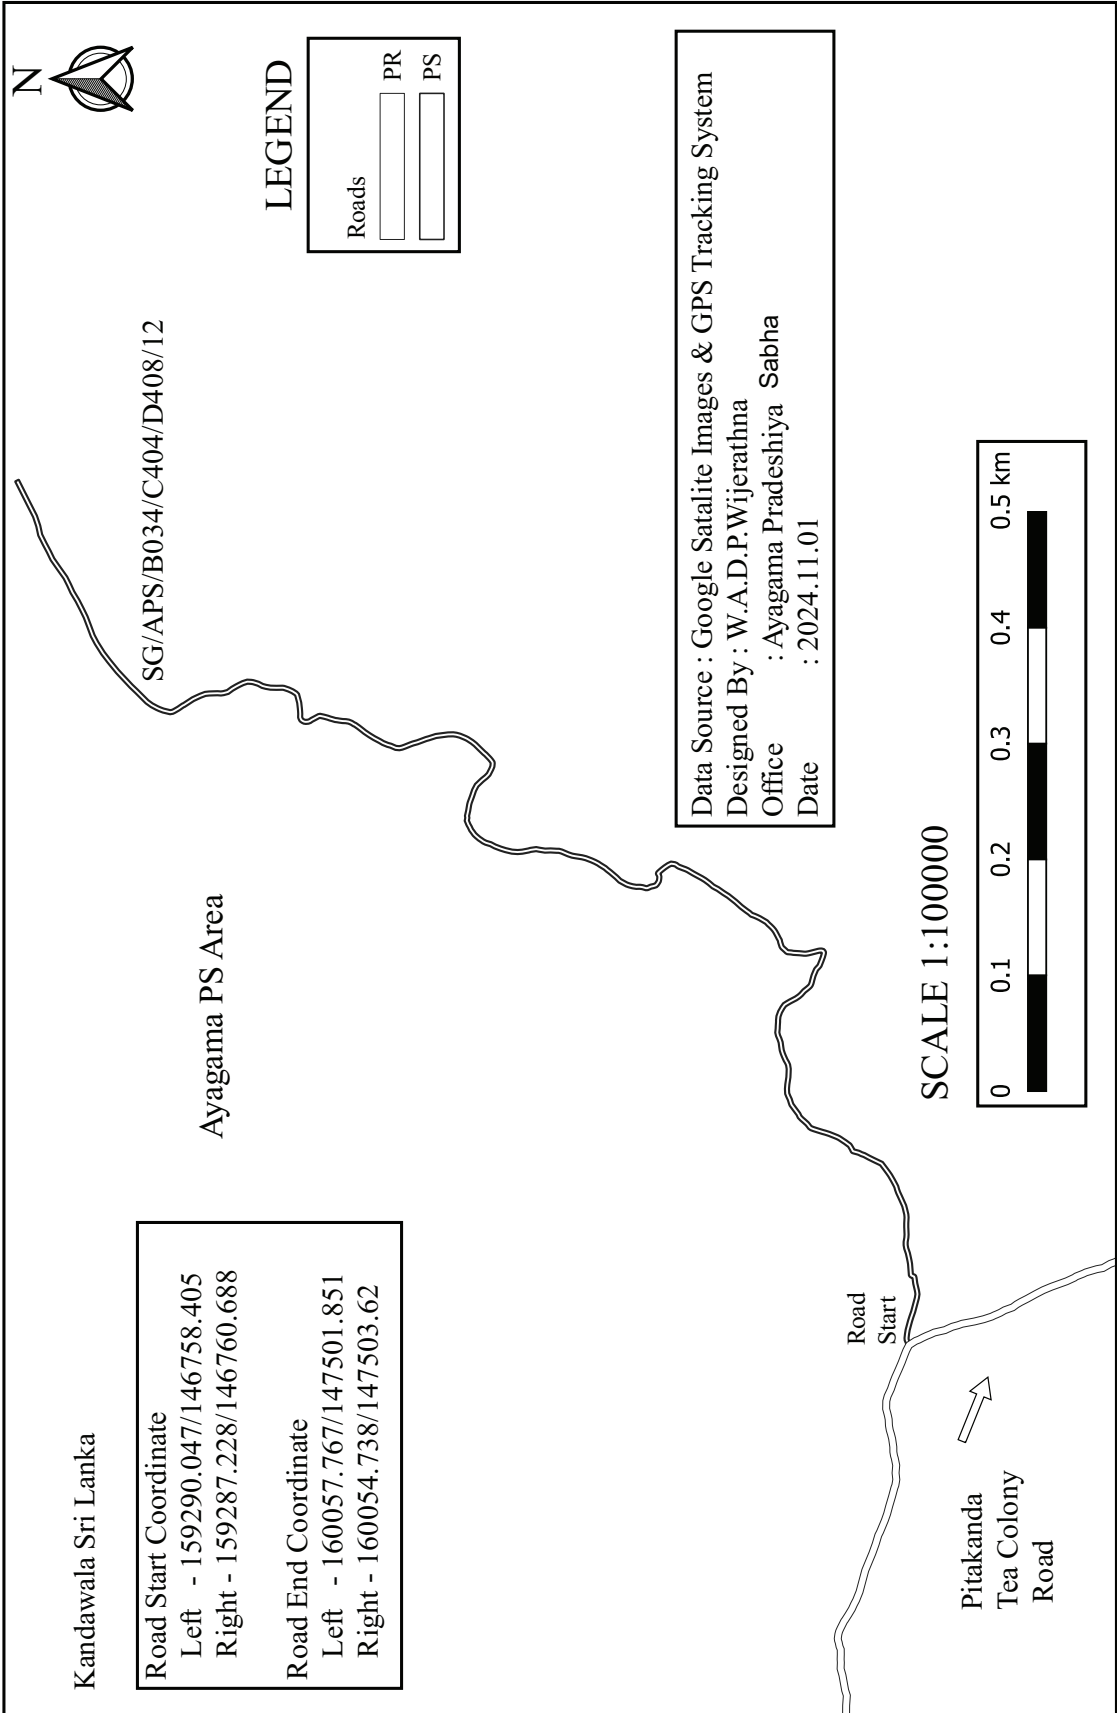


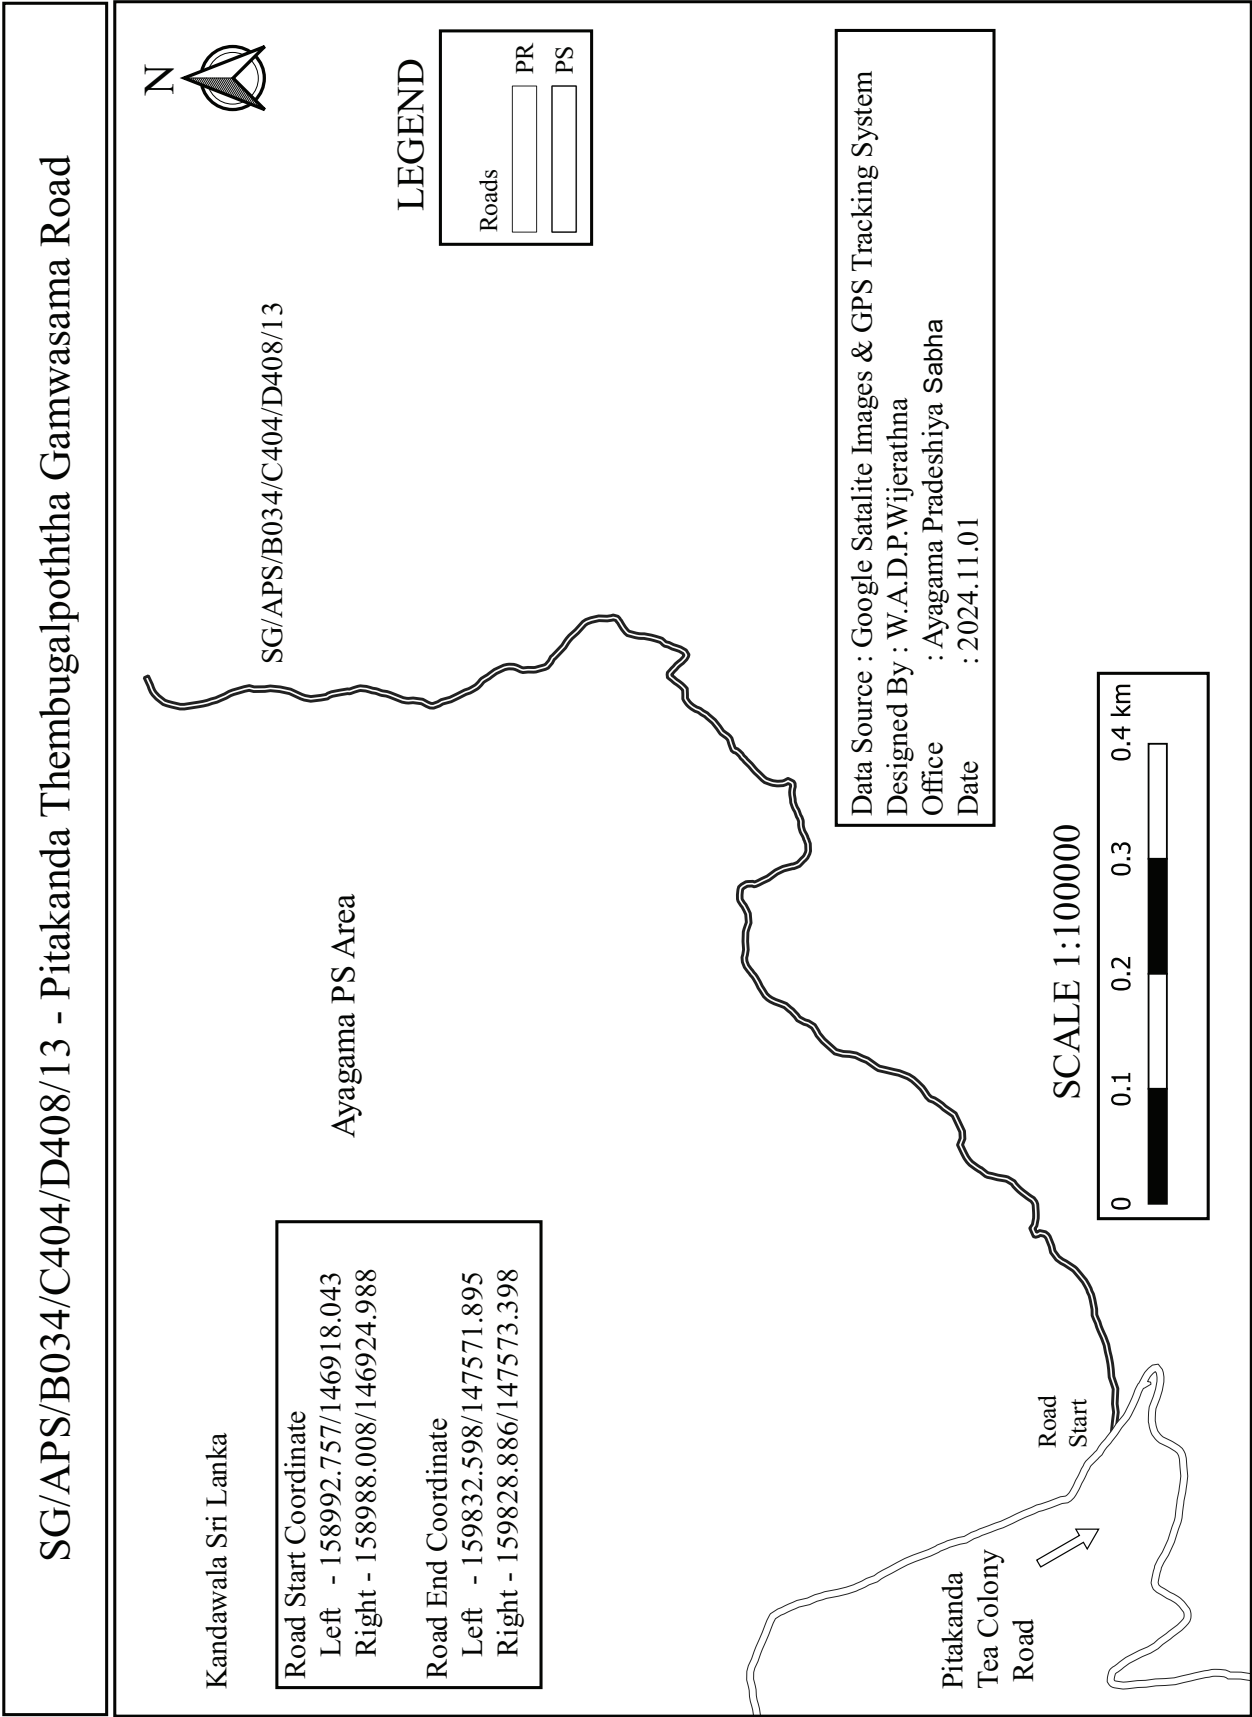


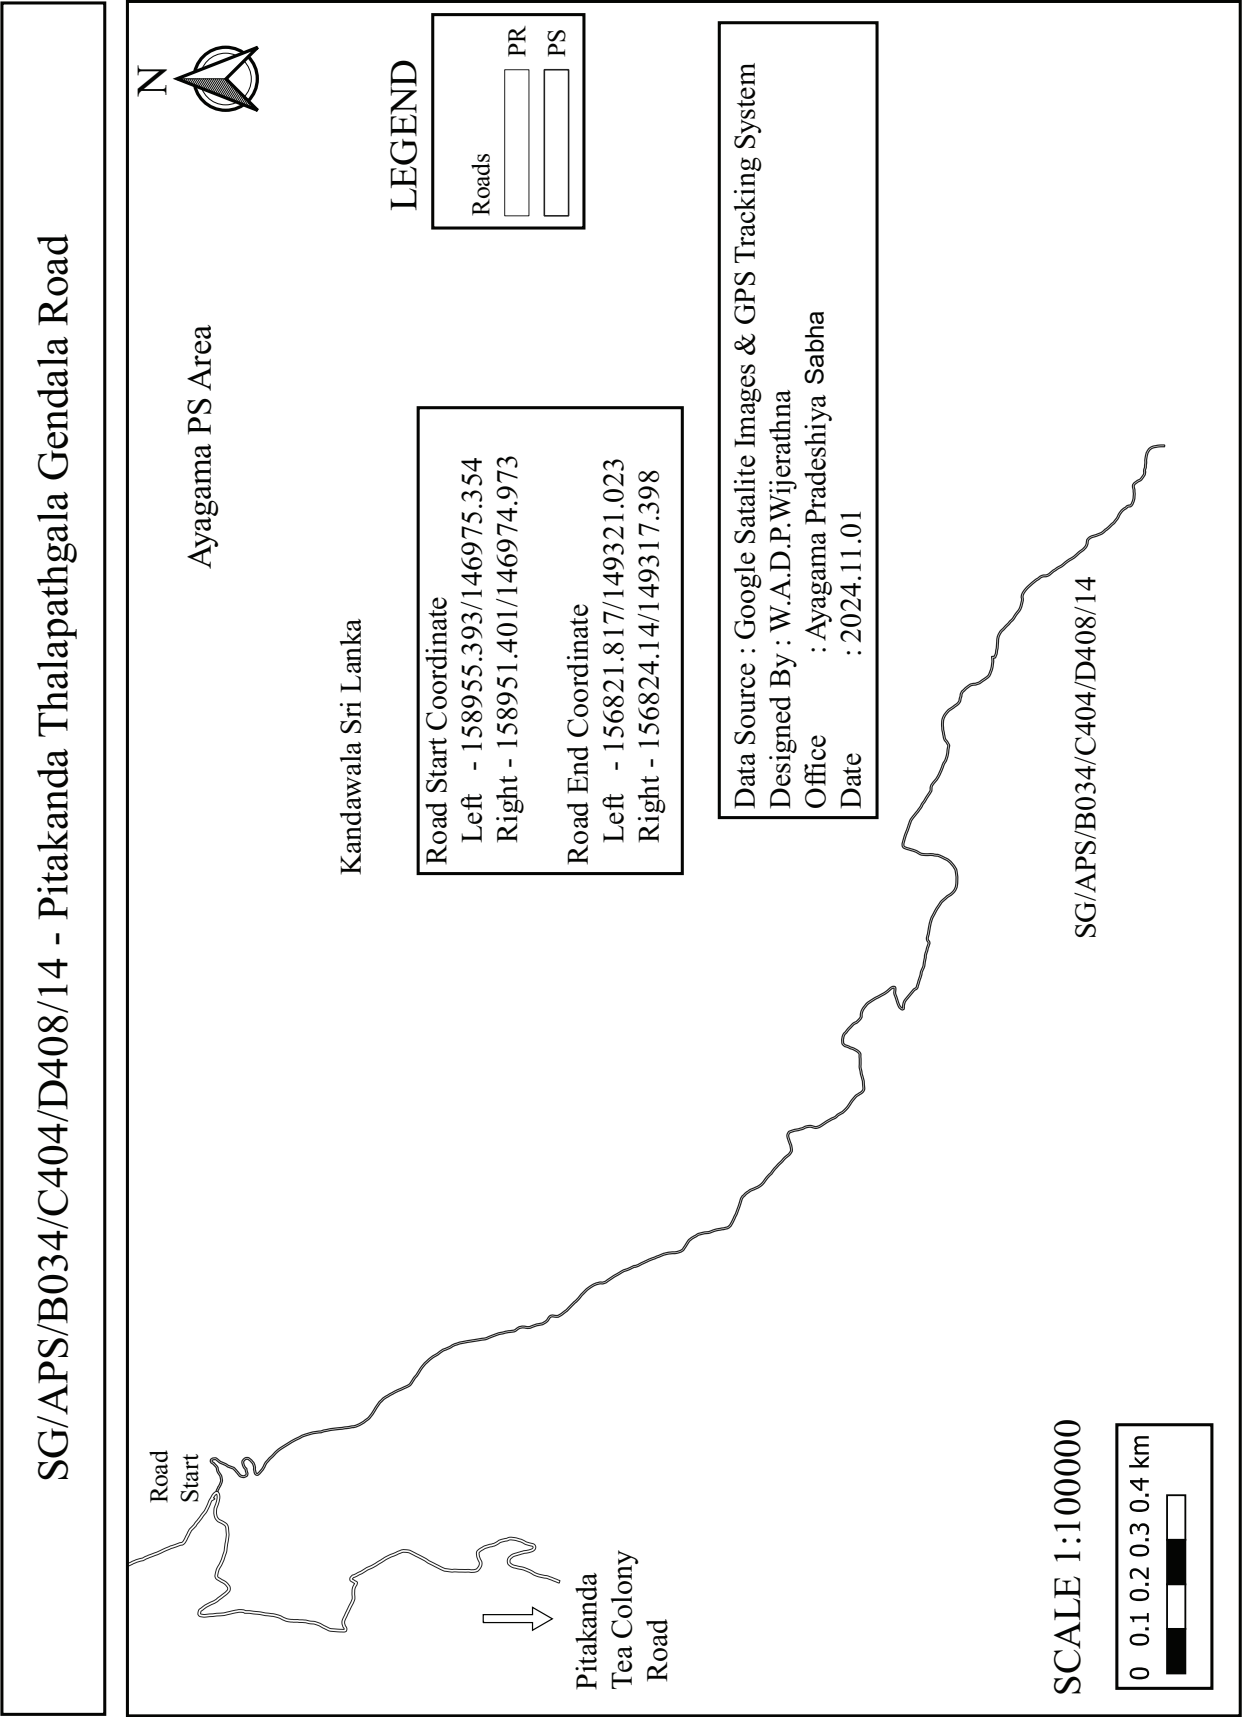

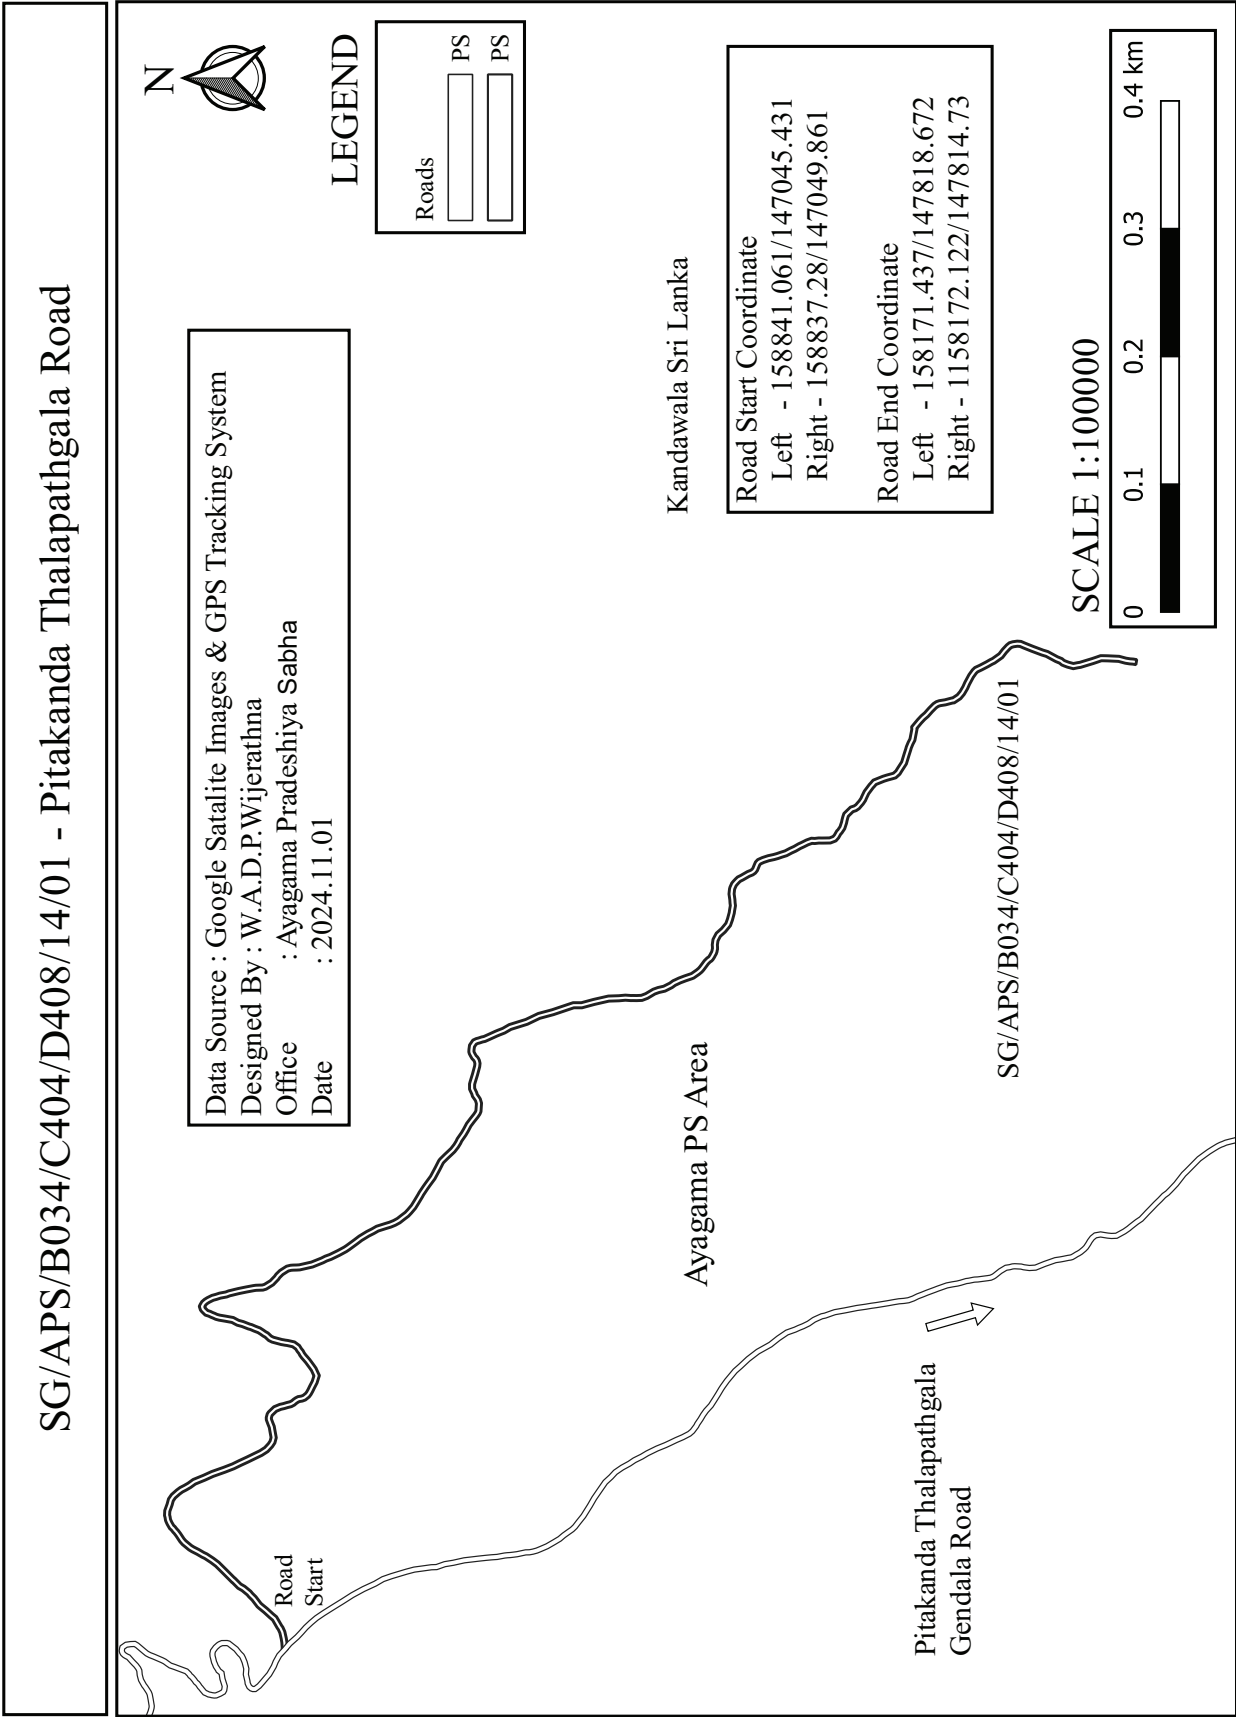



SG/APS/B034/C404/D408/14/02 - First Lane of Pitakanda Thalapathgala Road

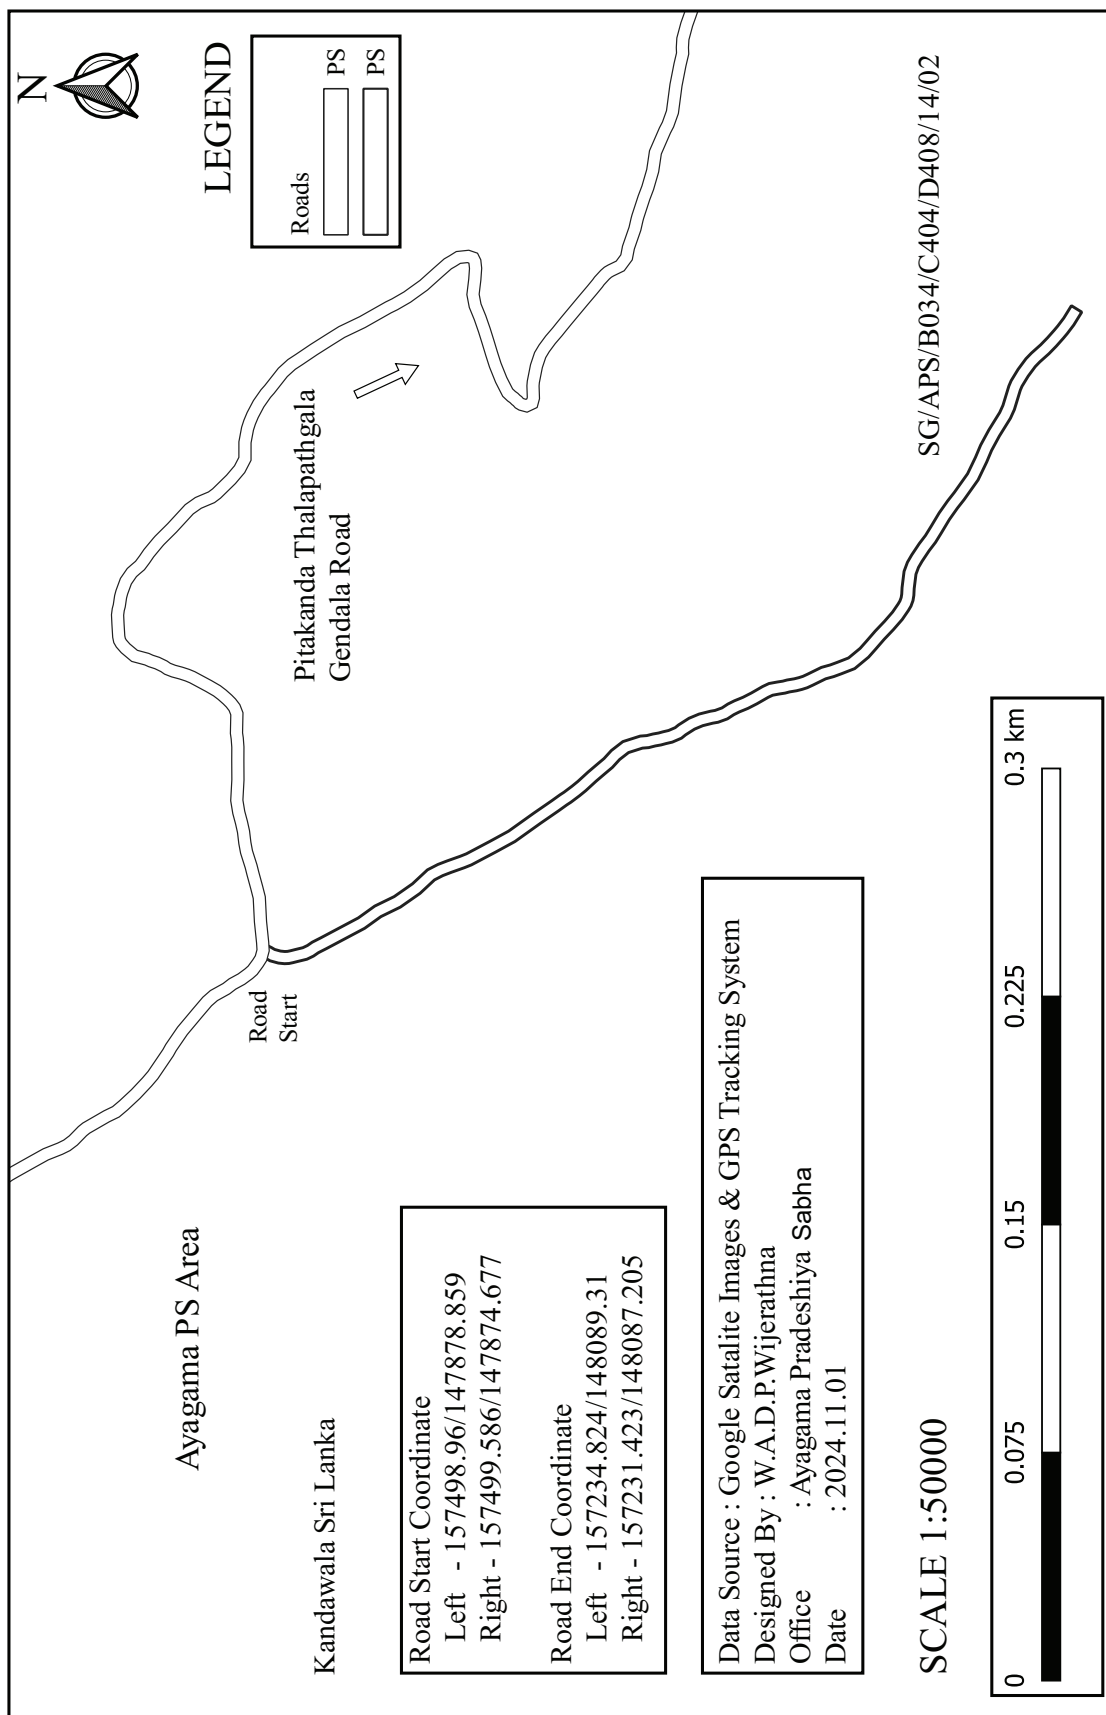


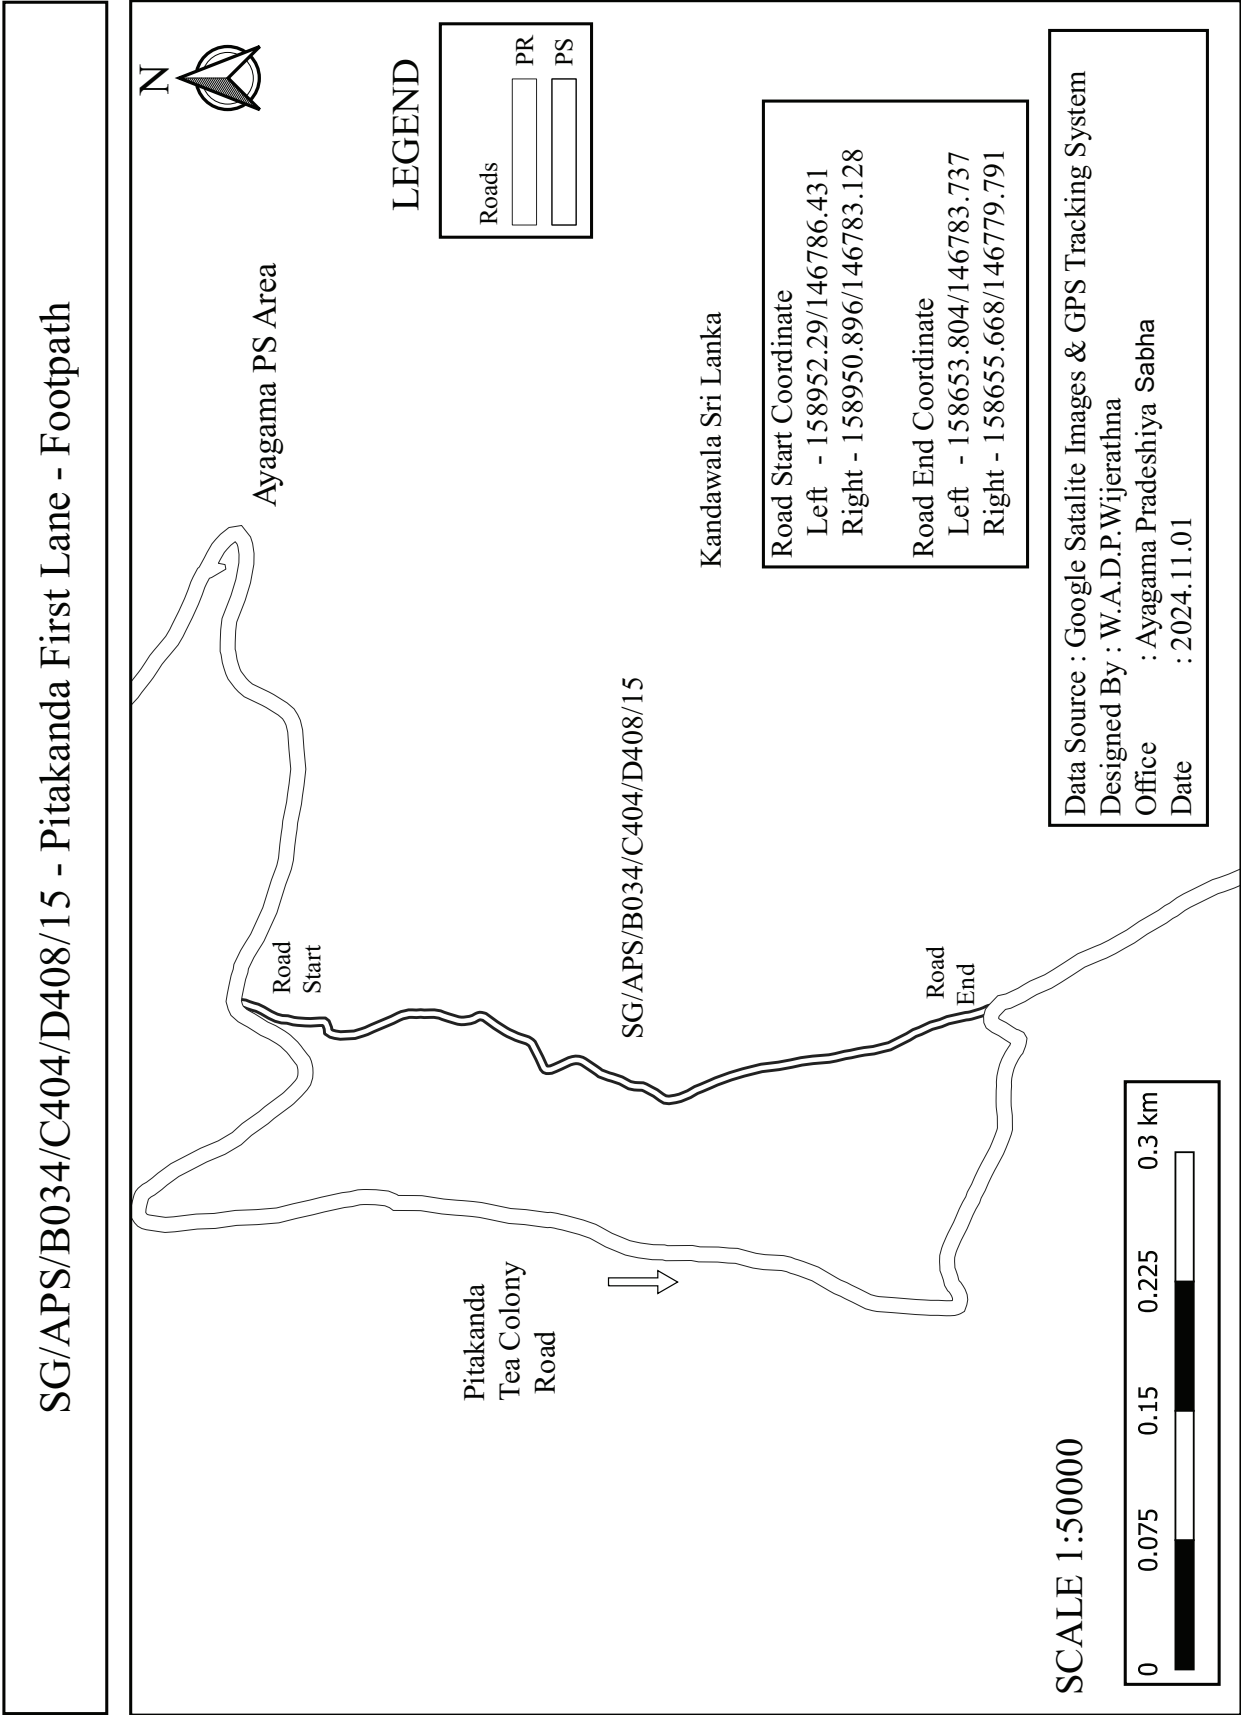



SG/APS/B034/C404/D408/16 - Pitakanda Panwilathenna Road

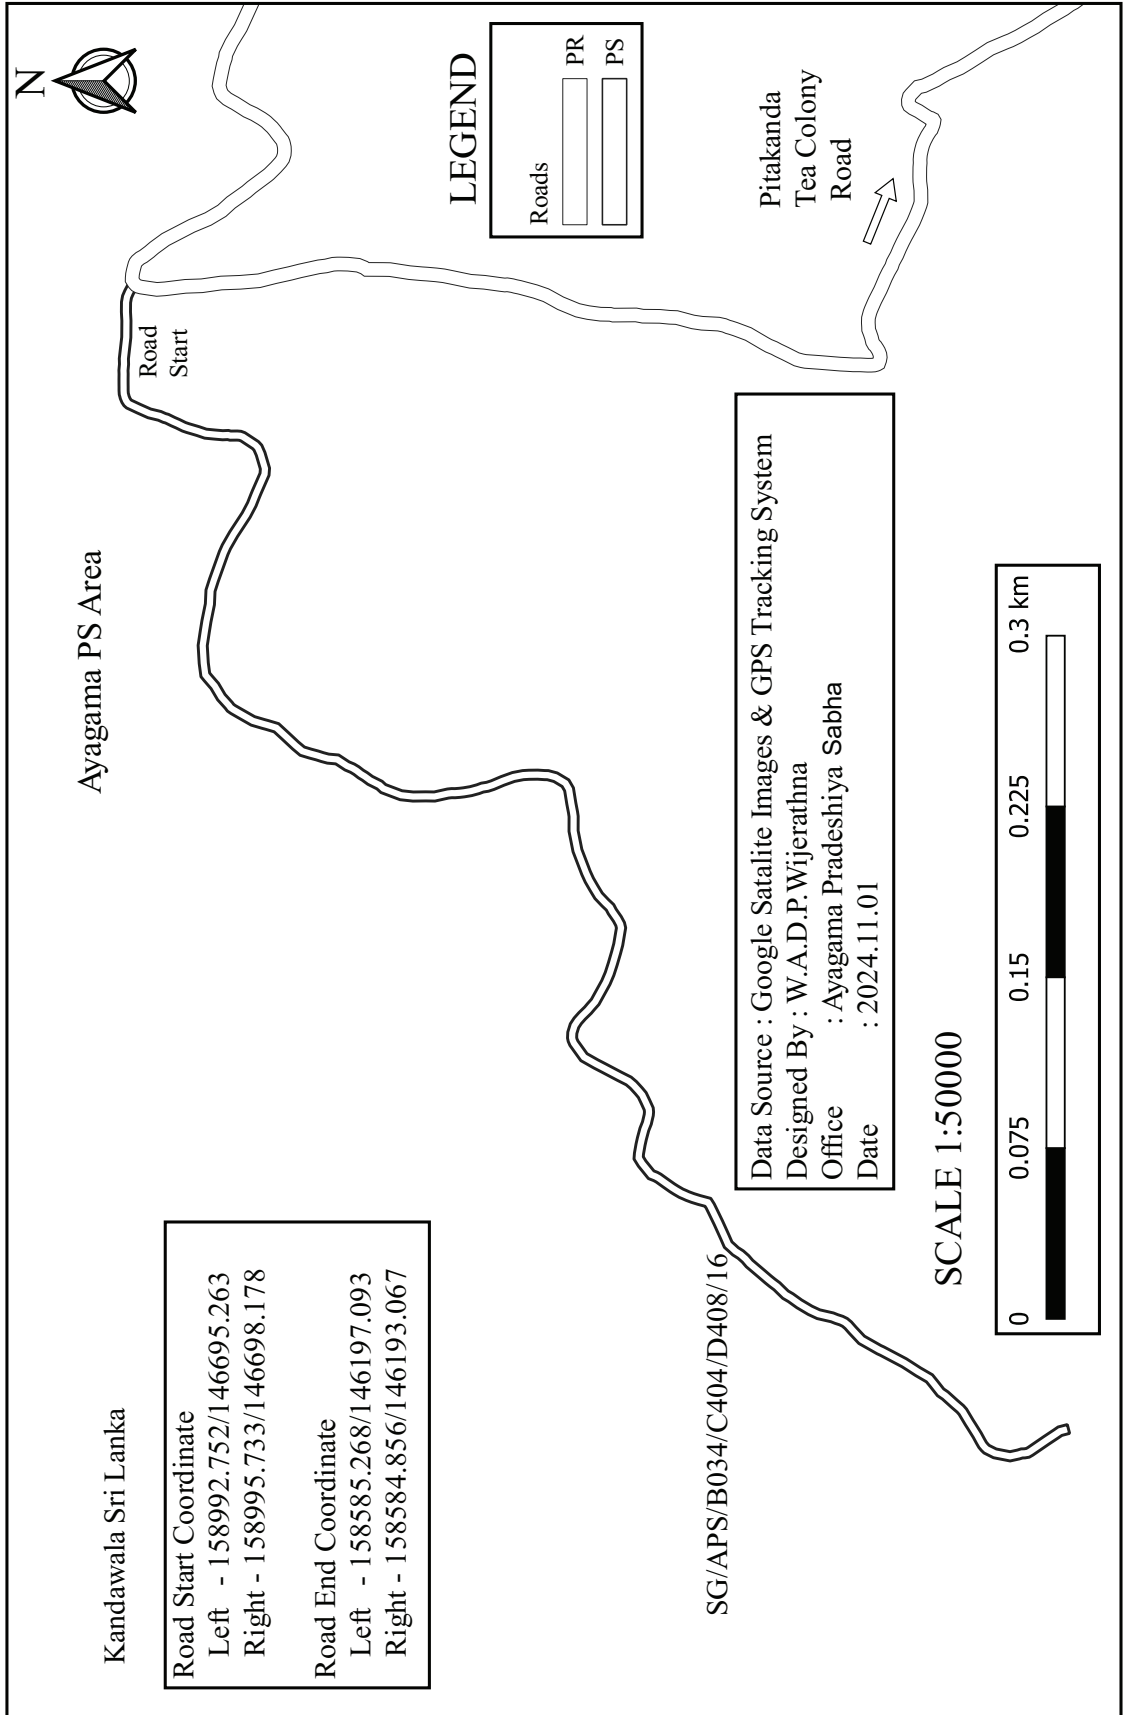


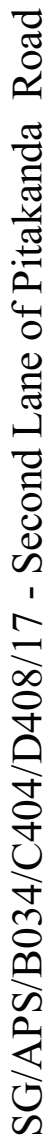

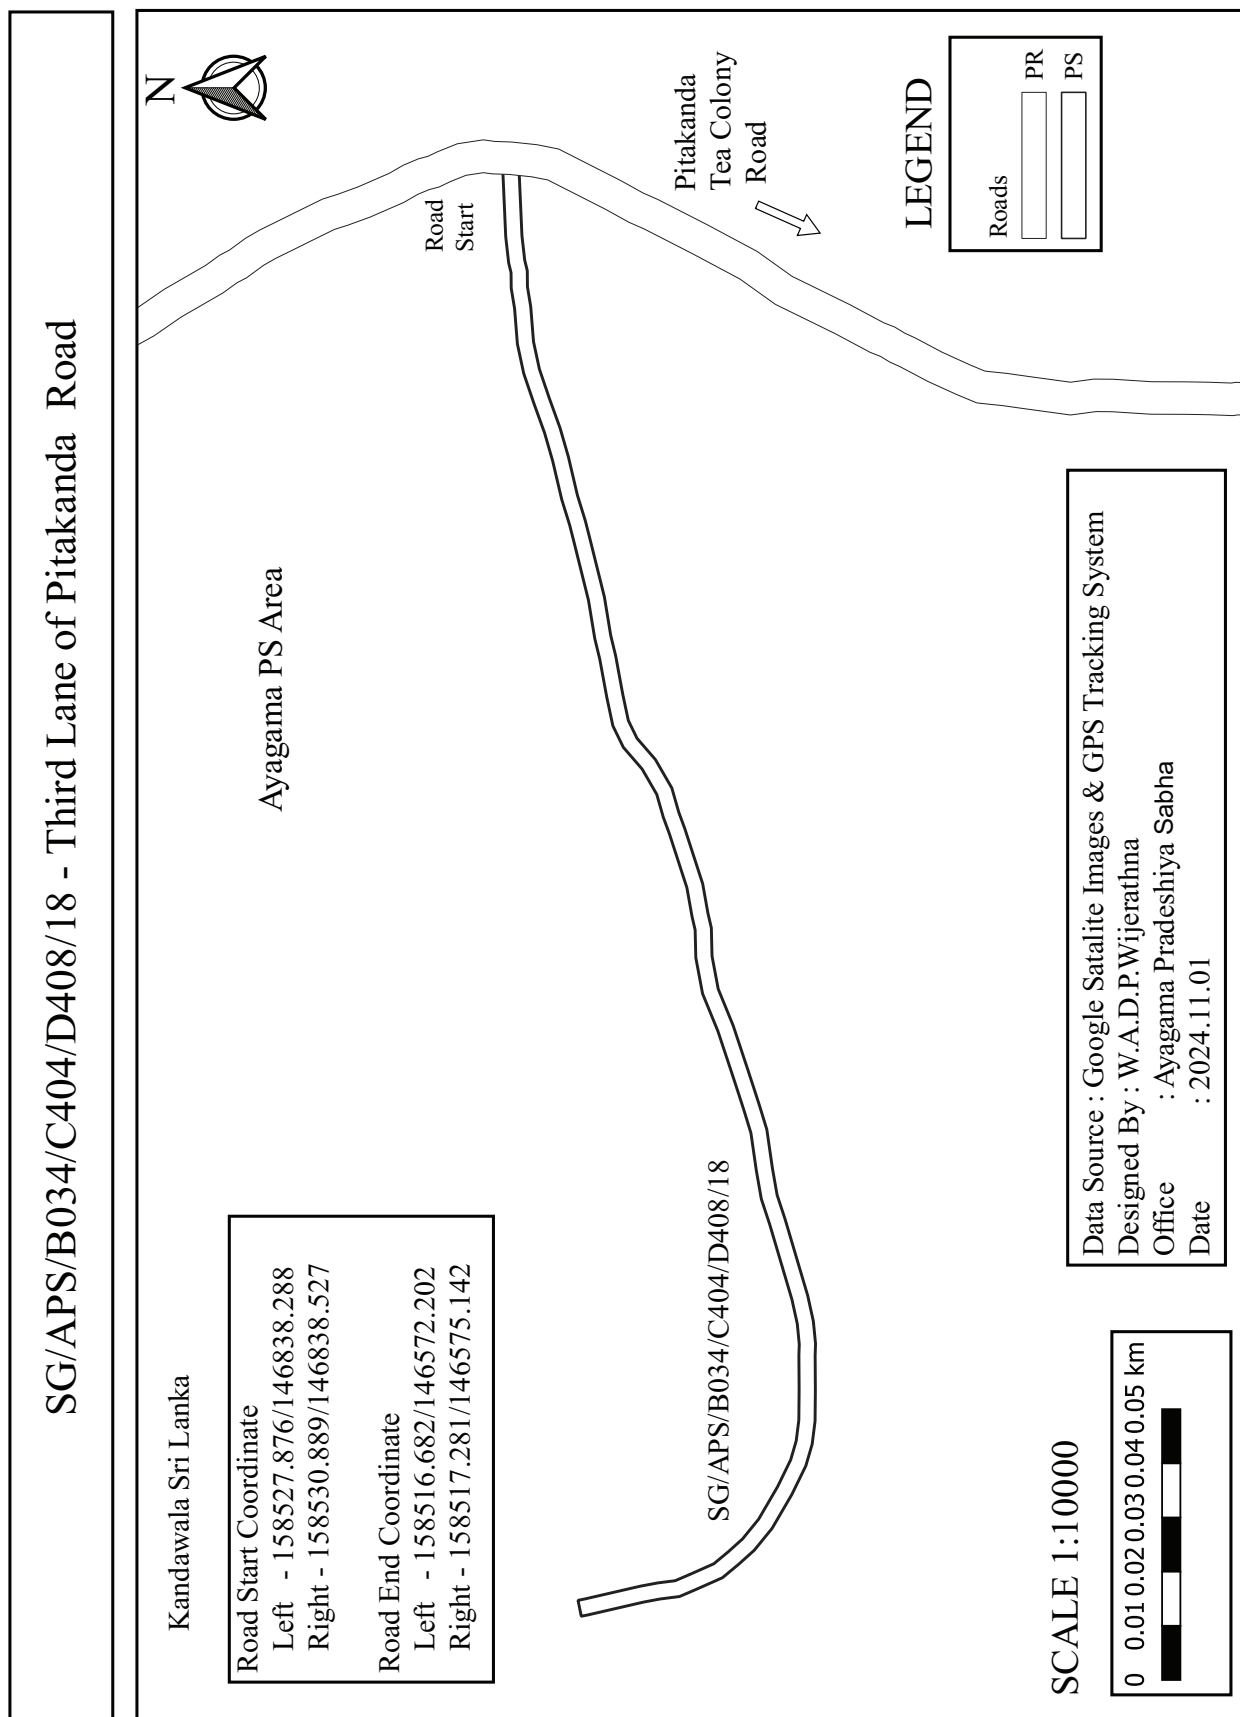


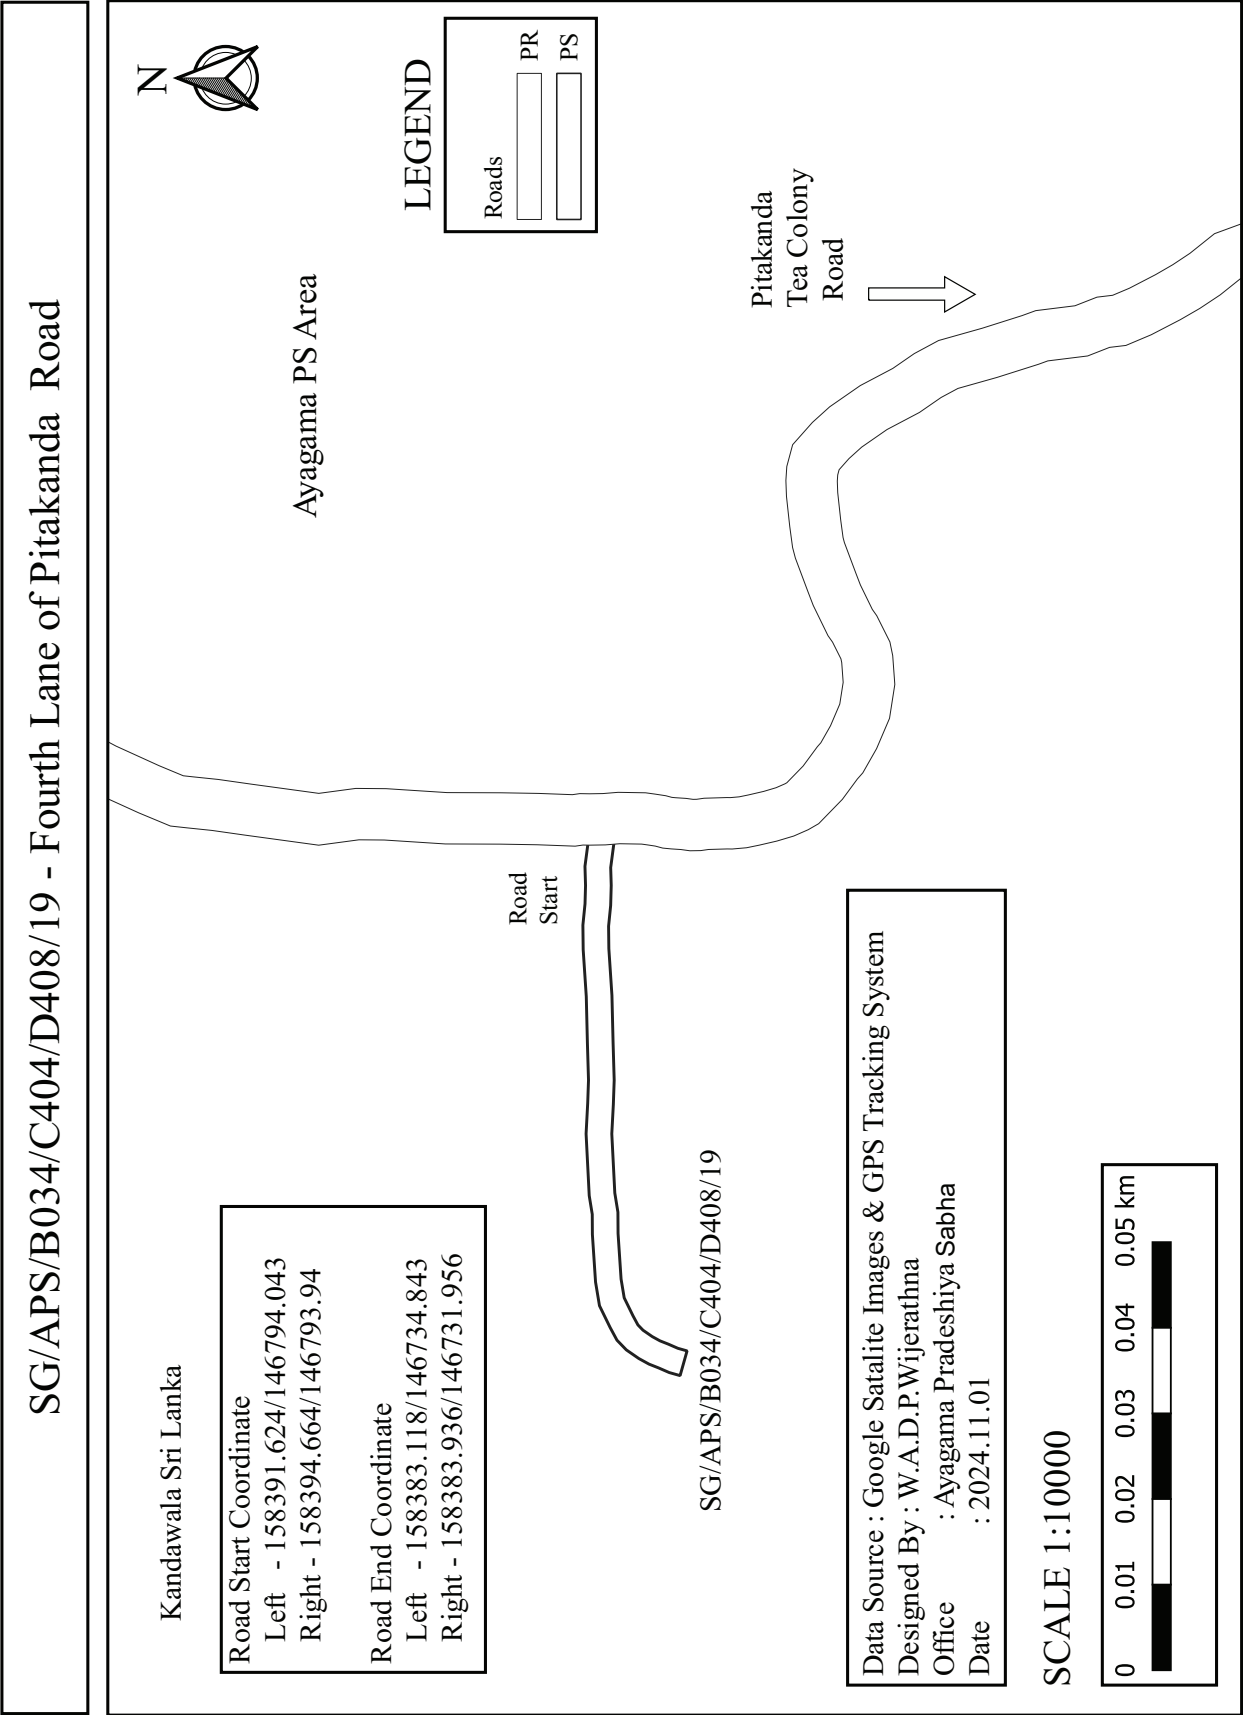


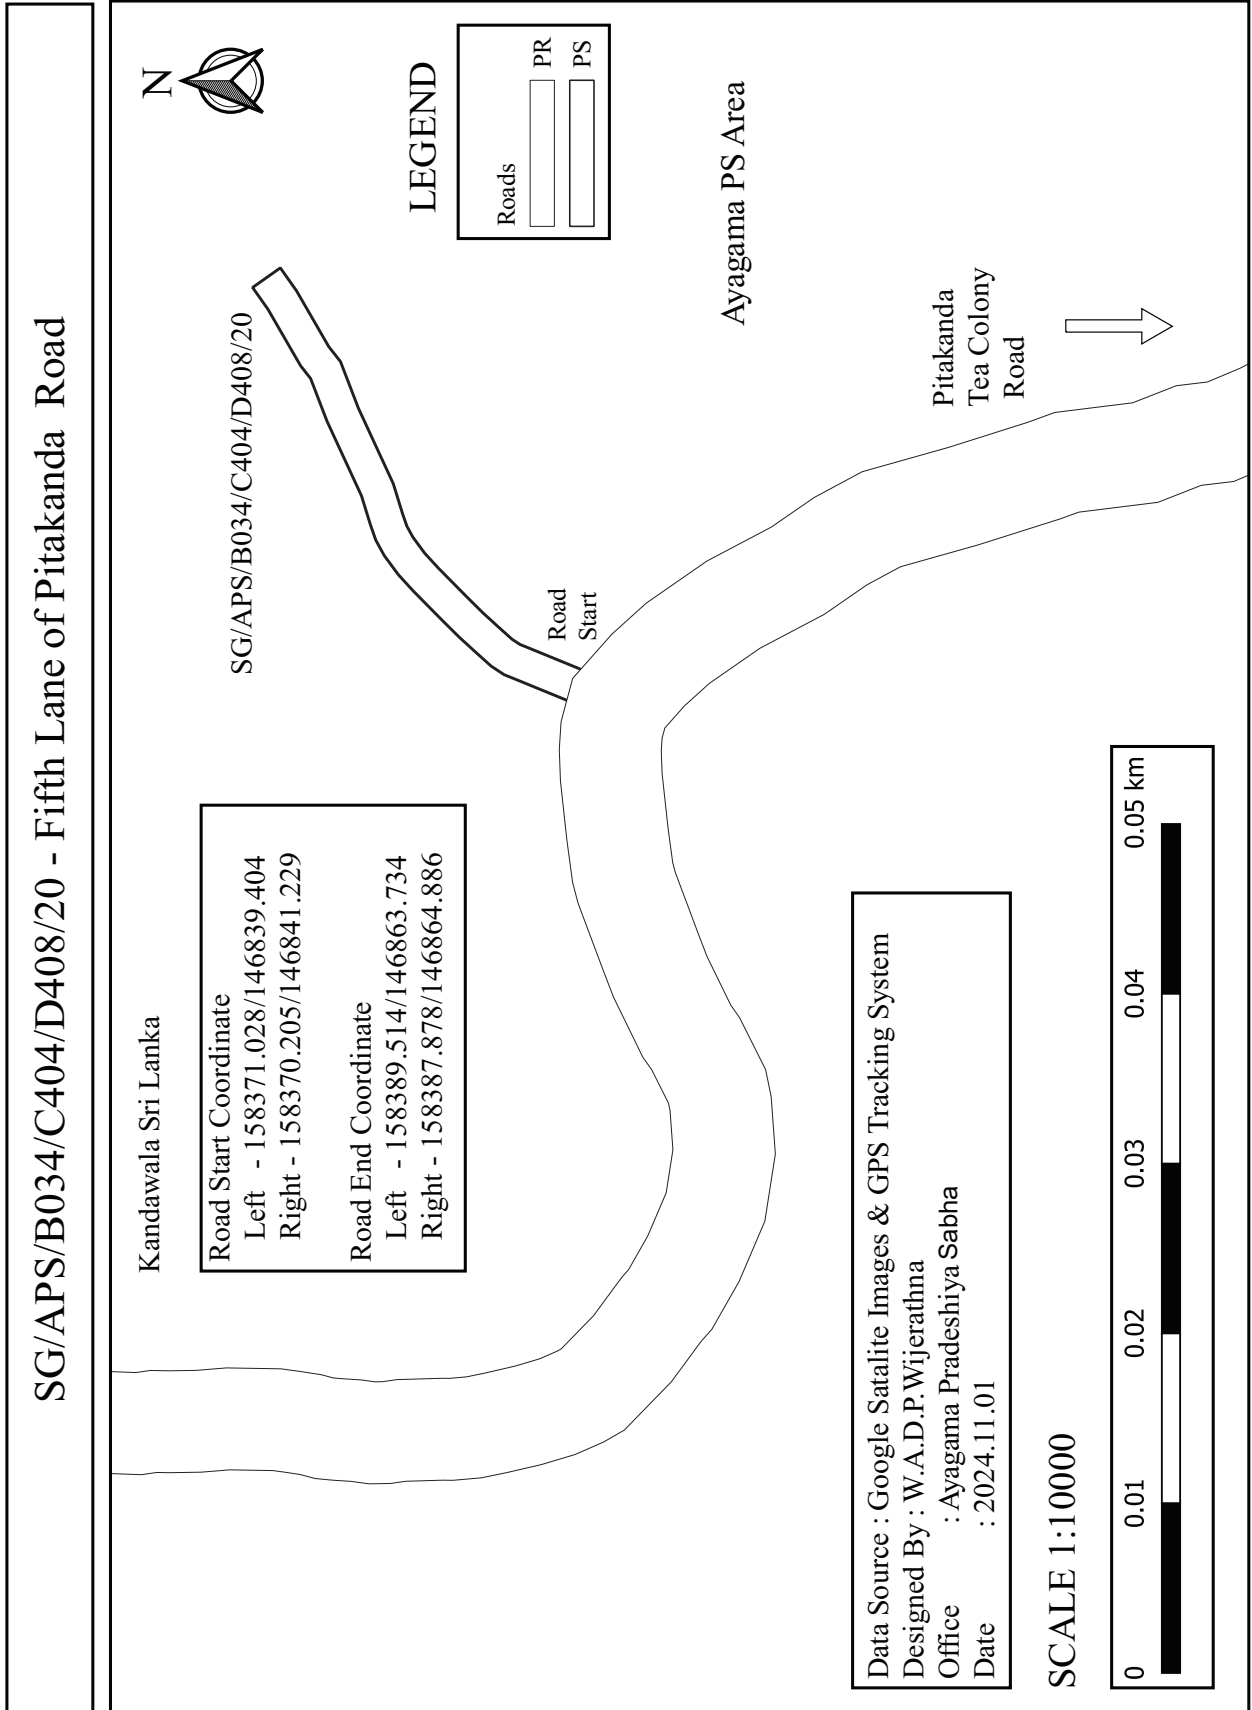

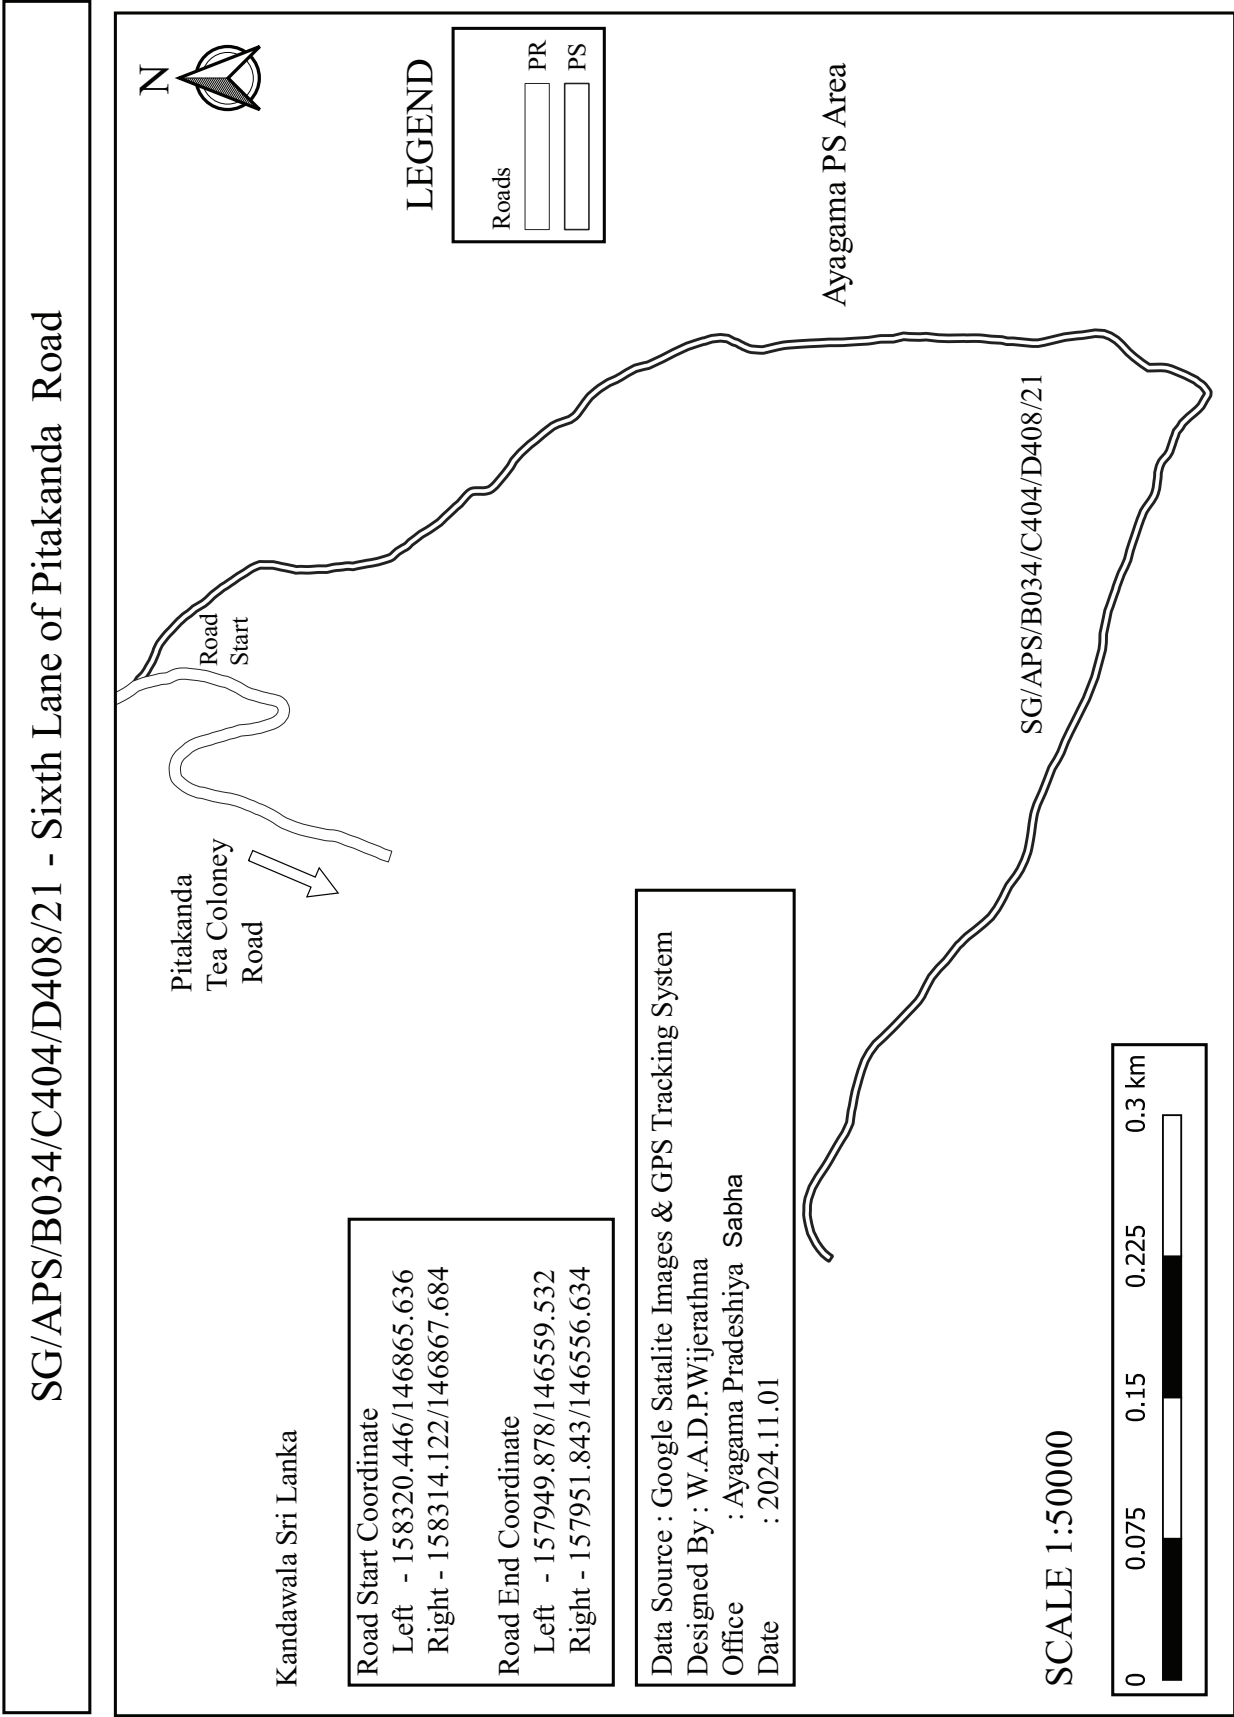



SG/APS/B034/C404/D408/21/01 - First By Pass - Footpath of Sixth Lane of Pitakanda Road

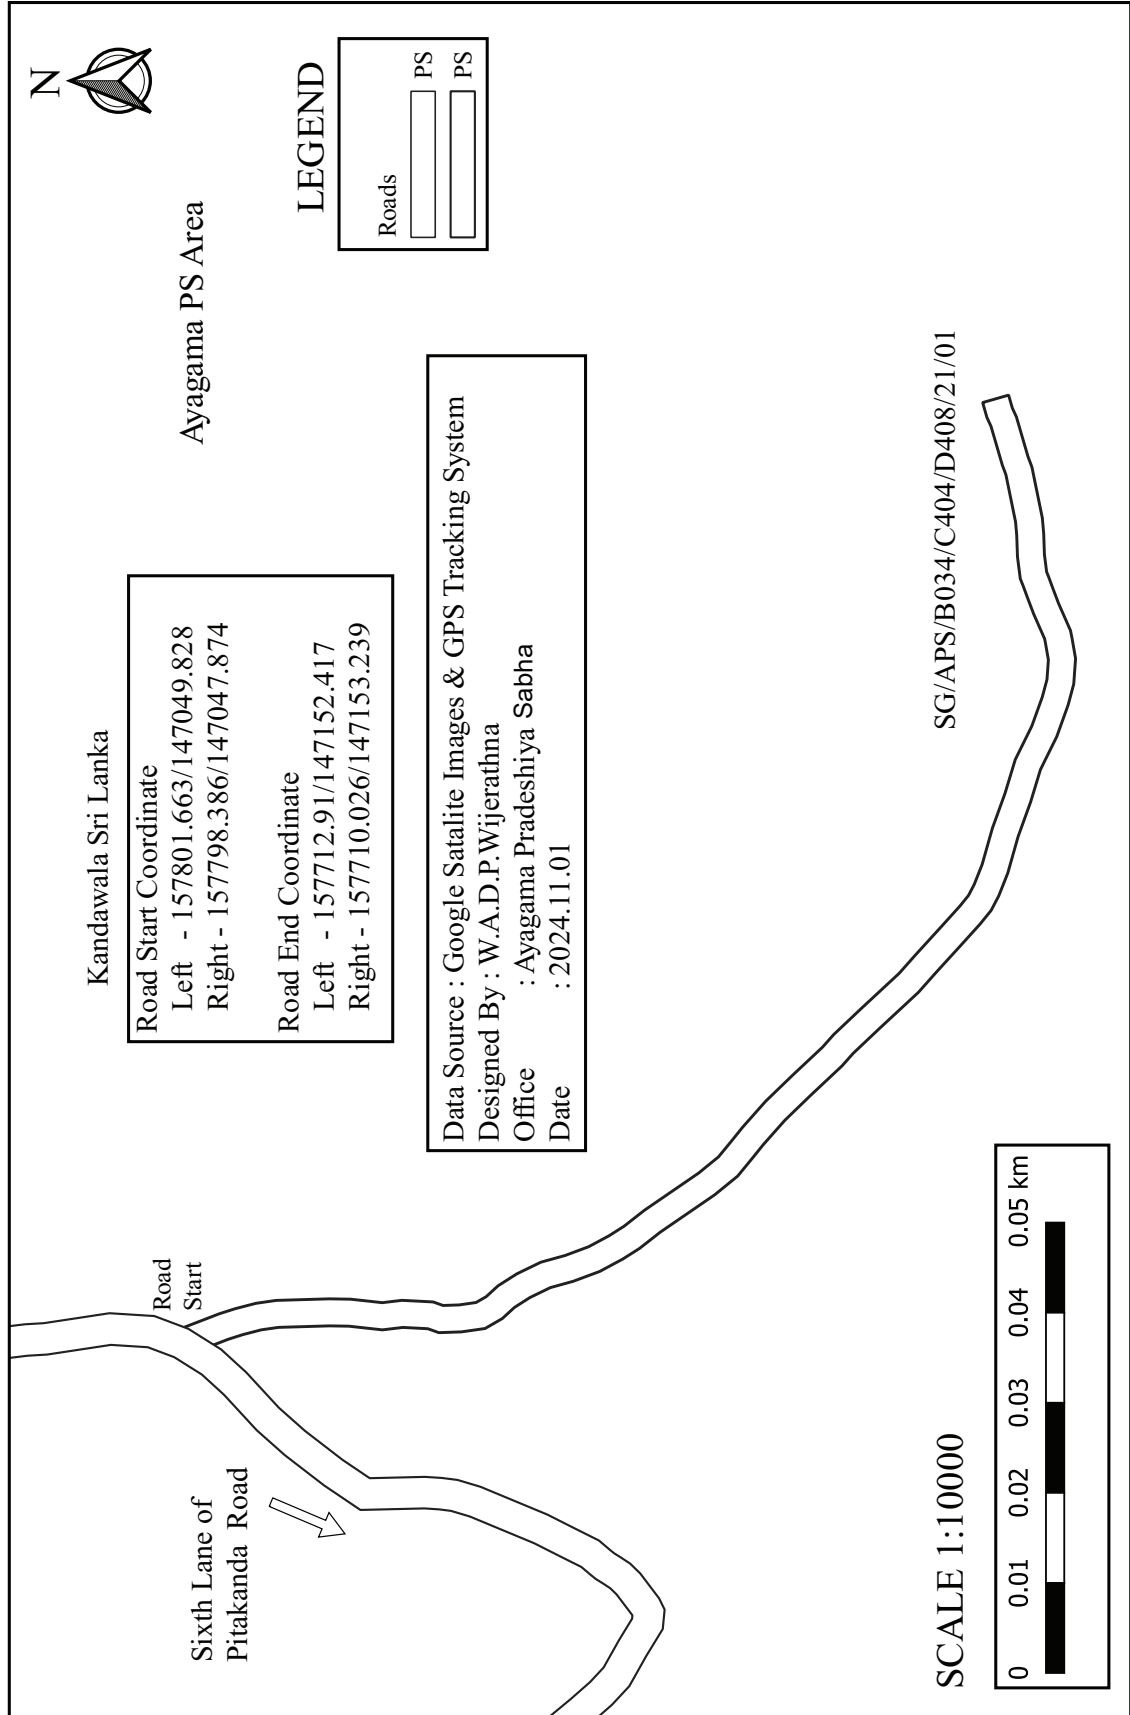


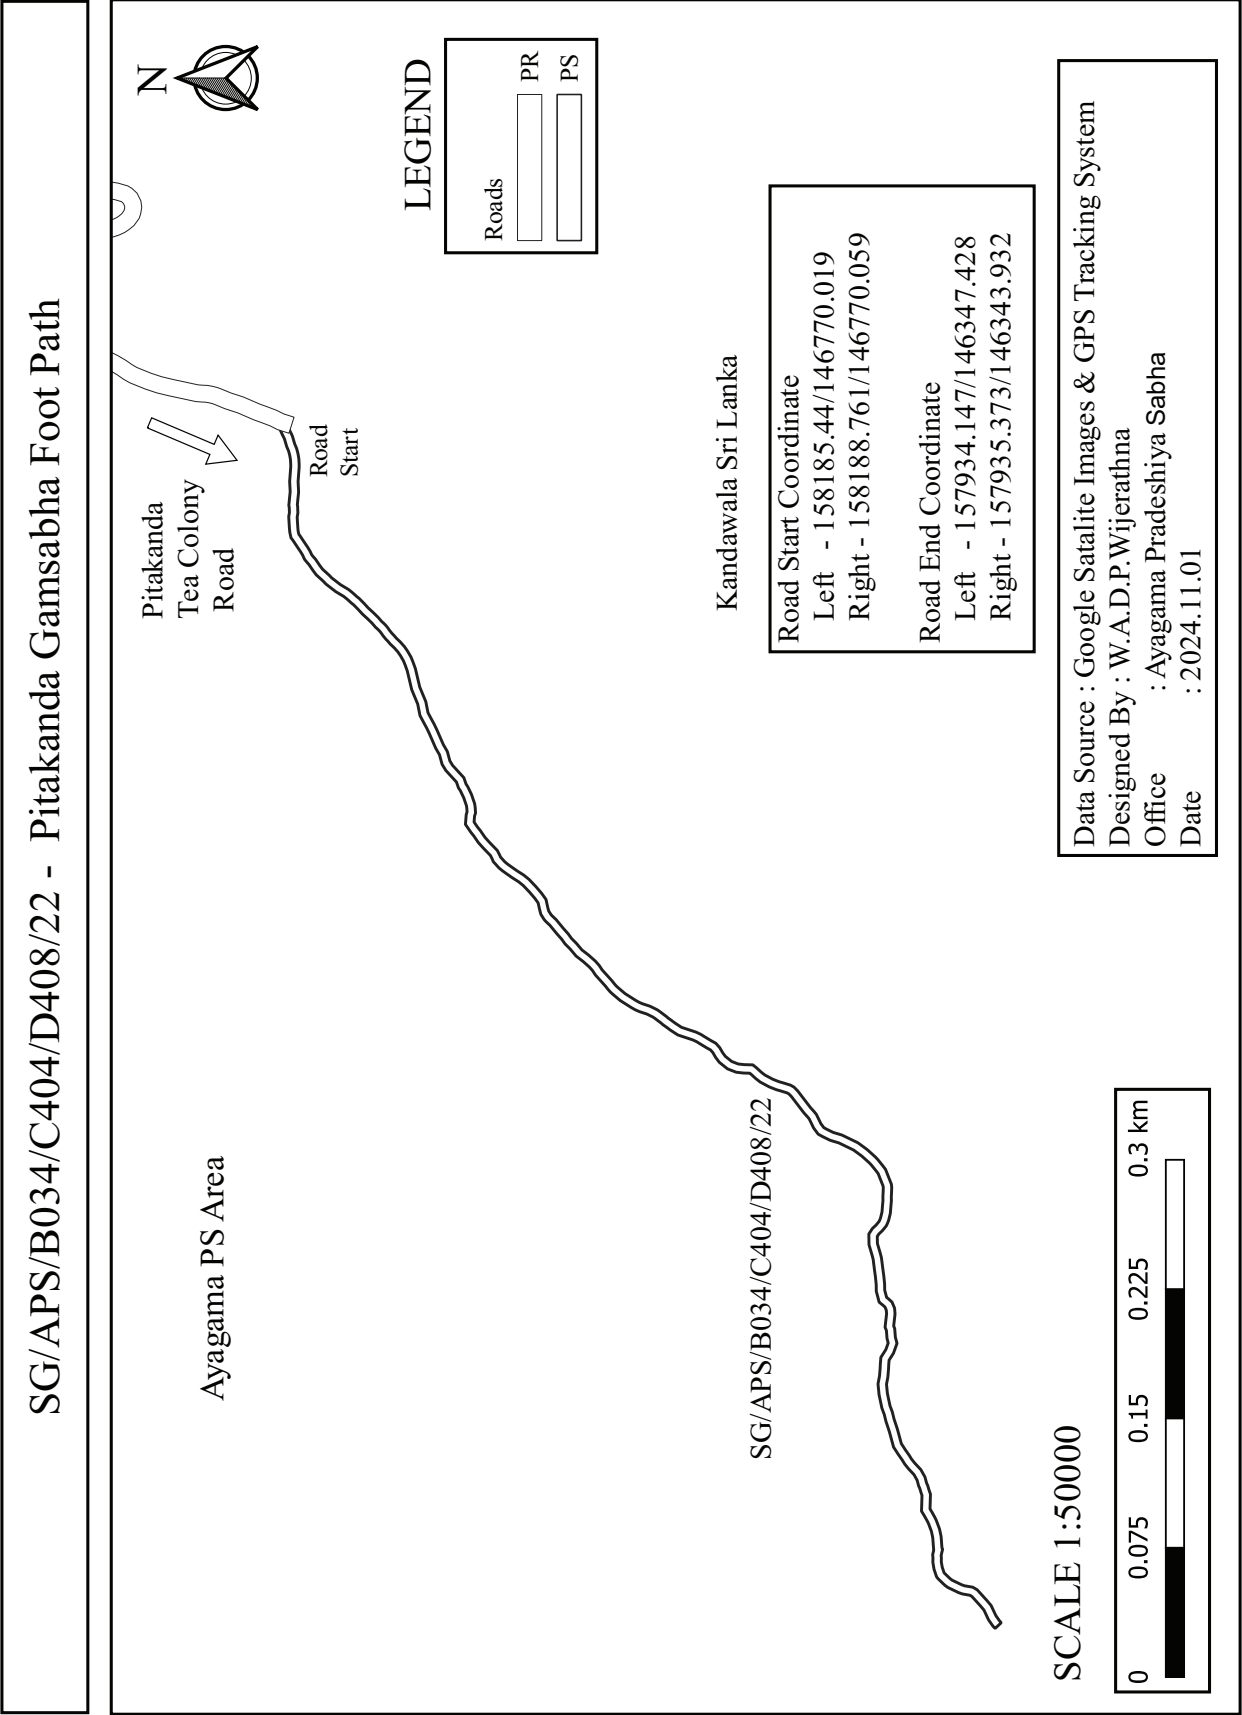


SG/APS/B034/C404/D408/23 - Seventh Lane of Pitakanda Road

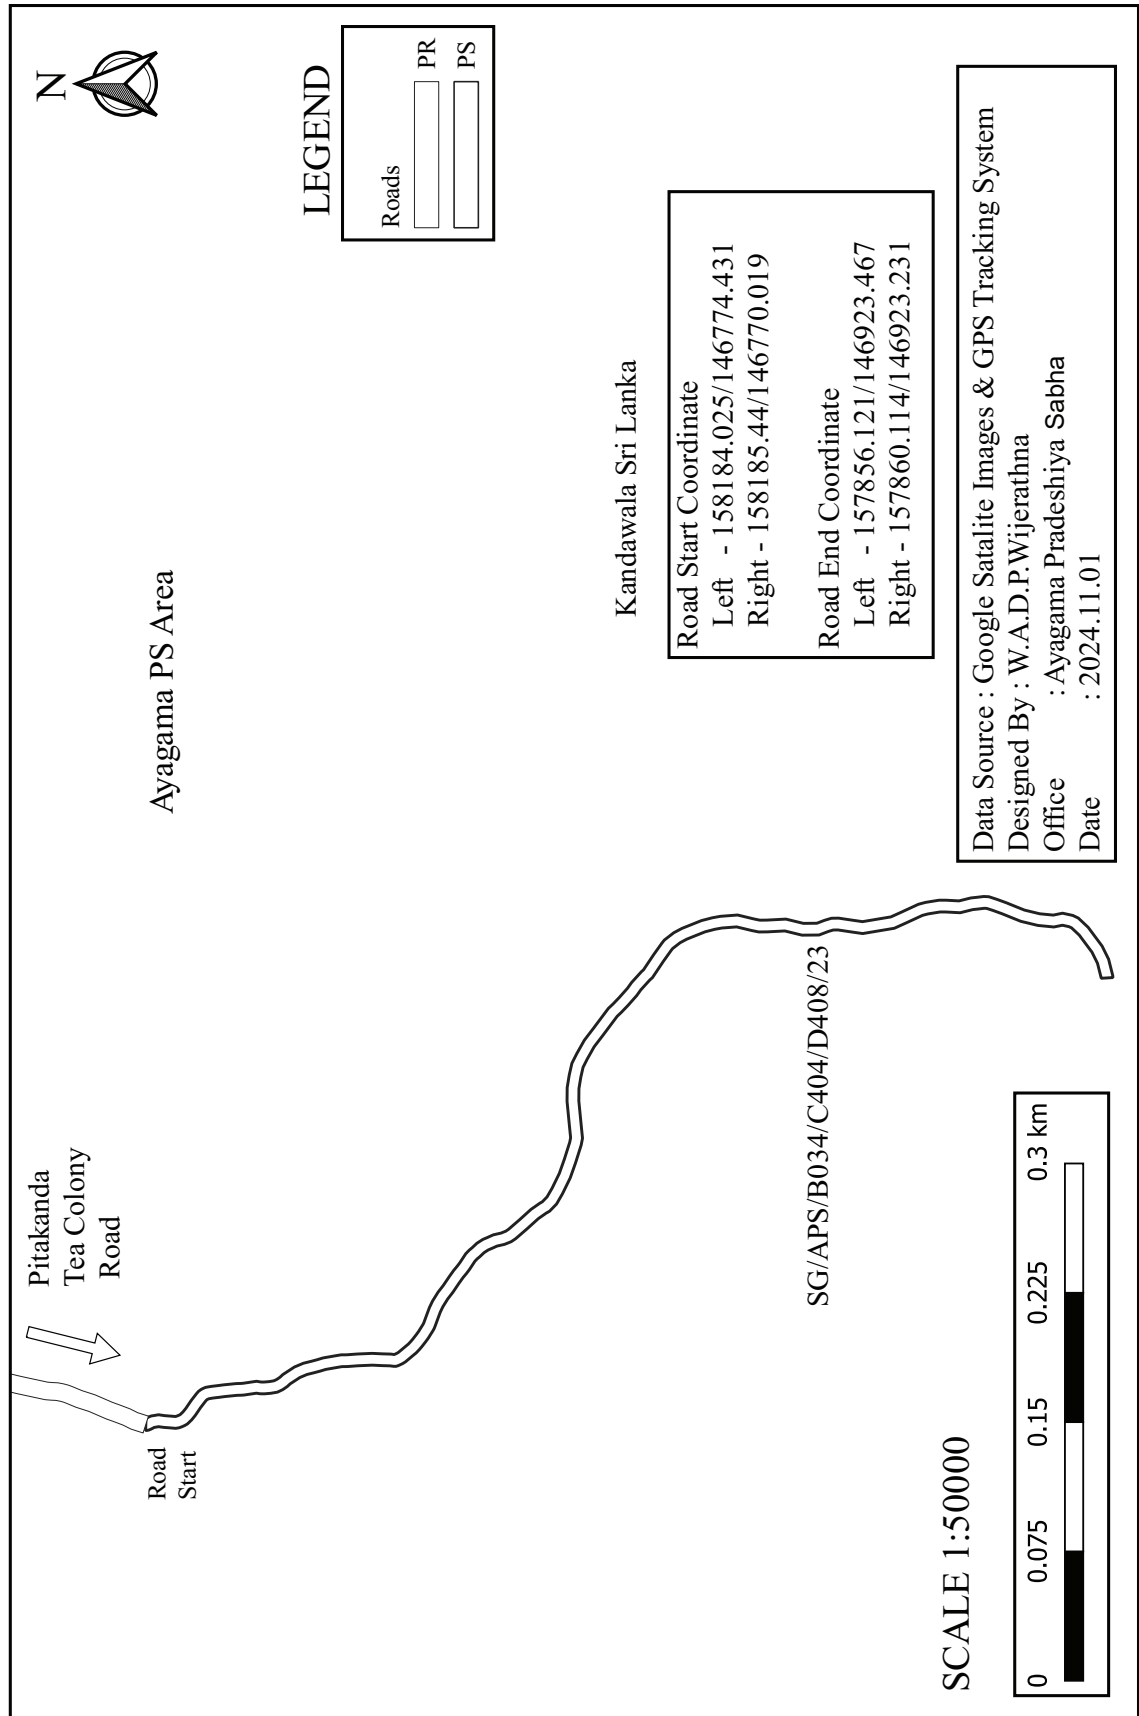


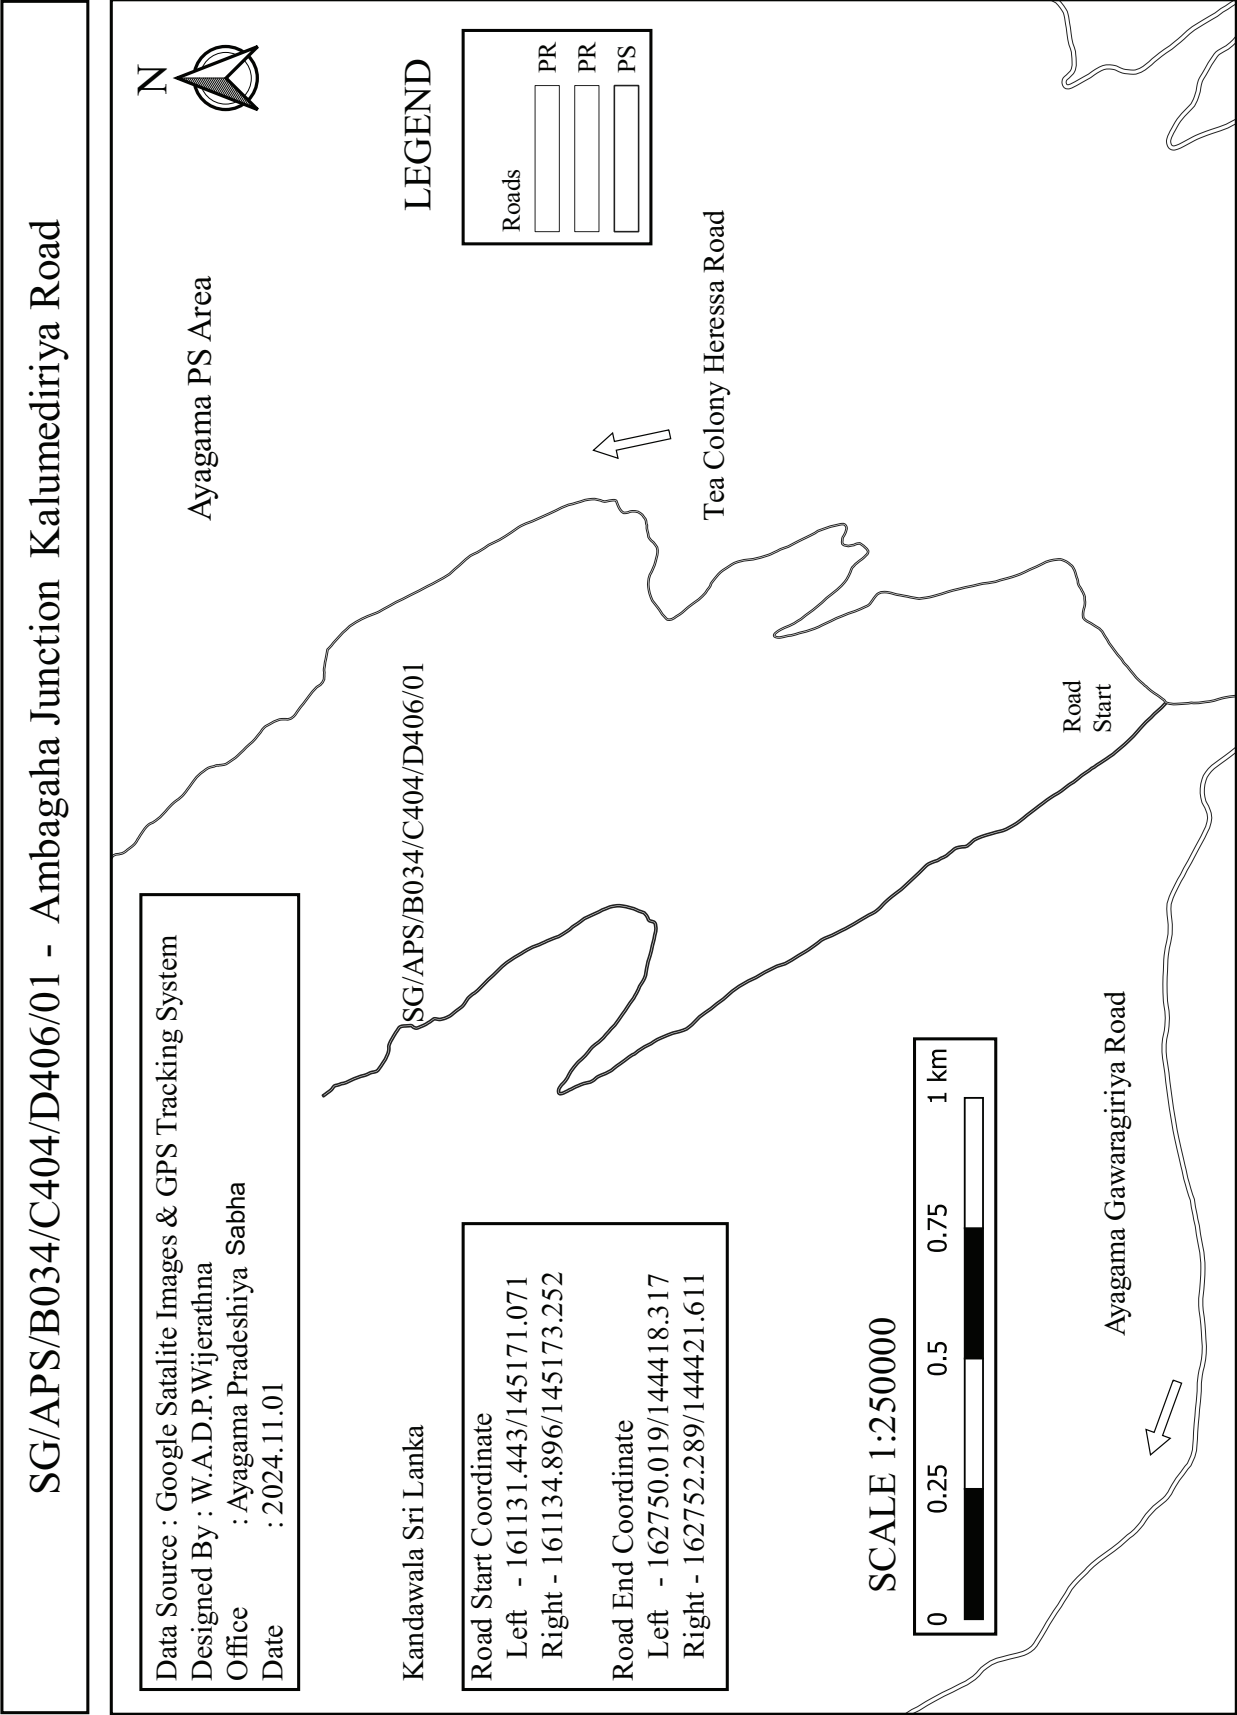

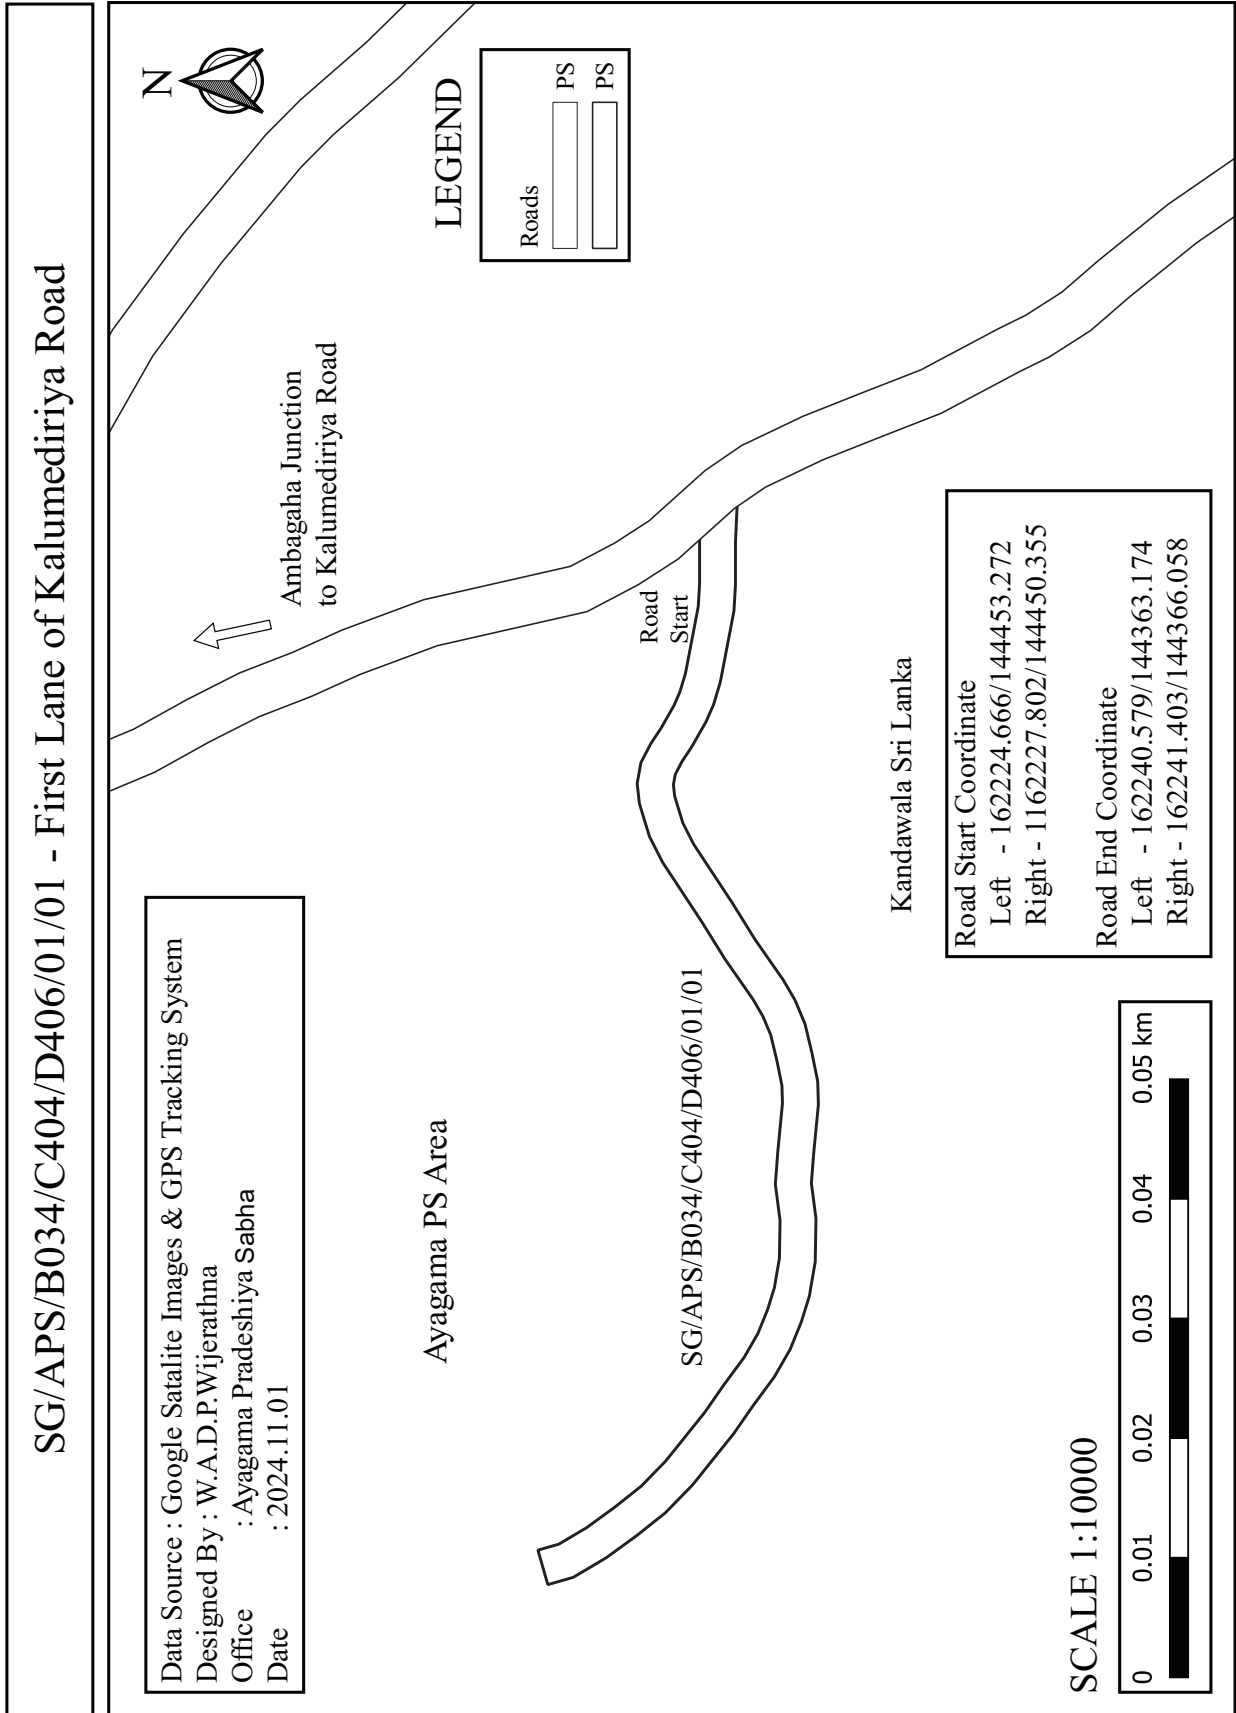



SG/APS/B034/C404/D406/01/02/01 - First Lane of Kalumediriya Teakanda Kuttikanda Road

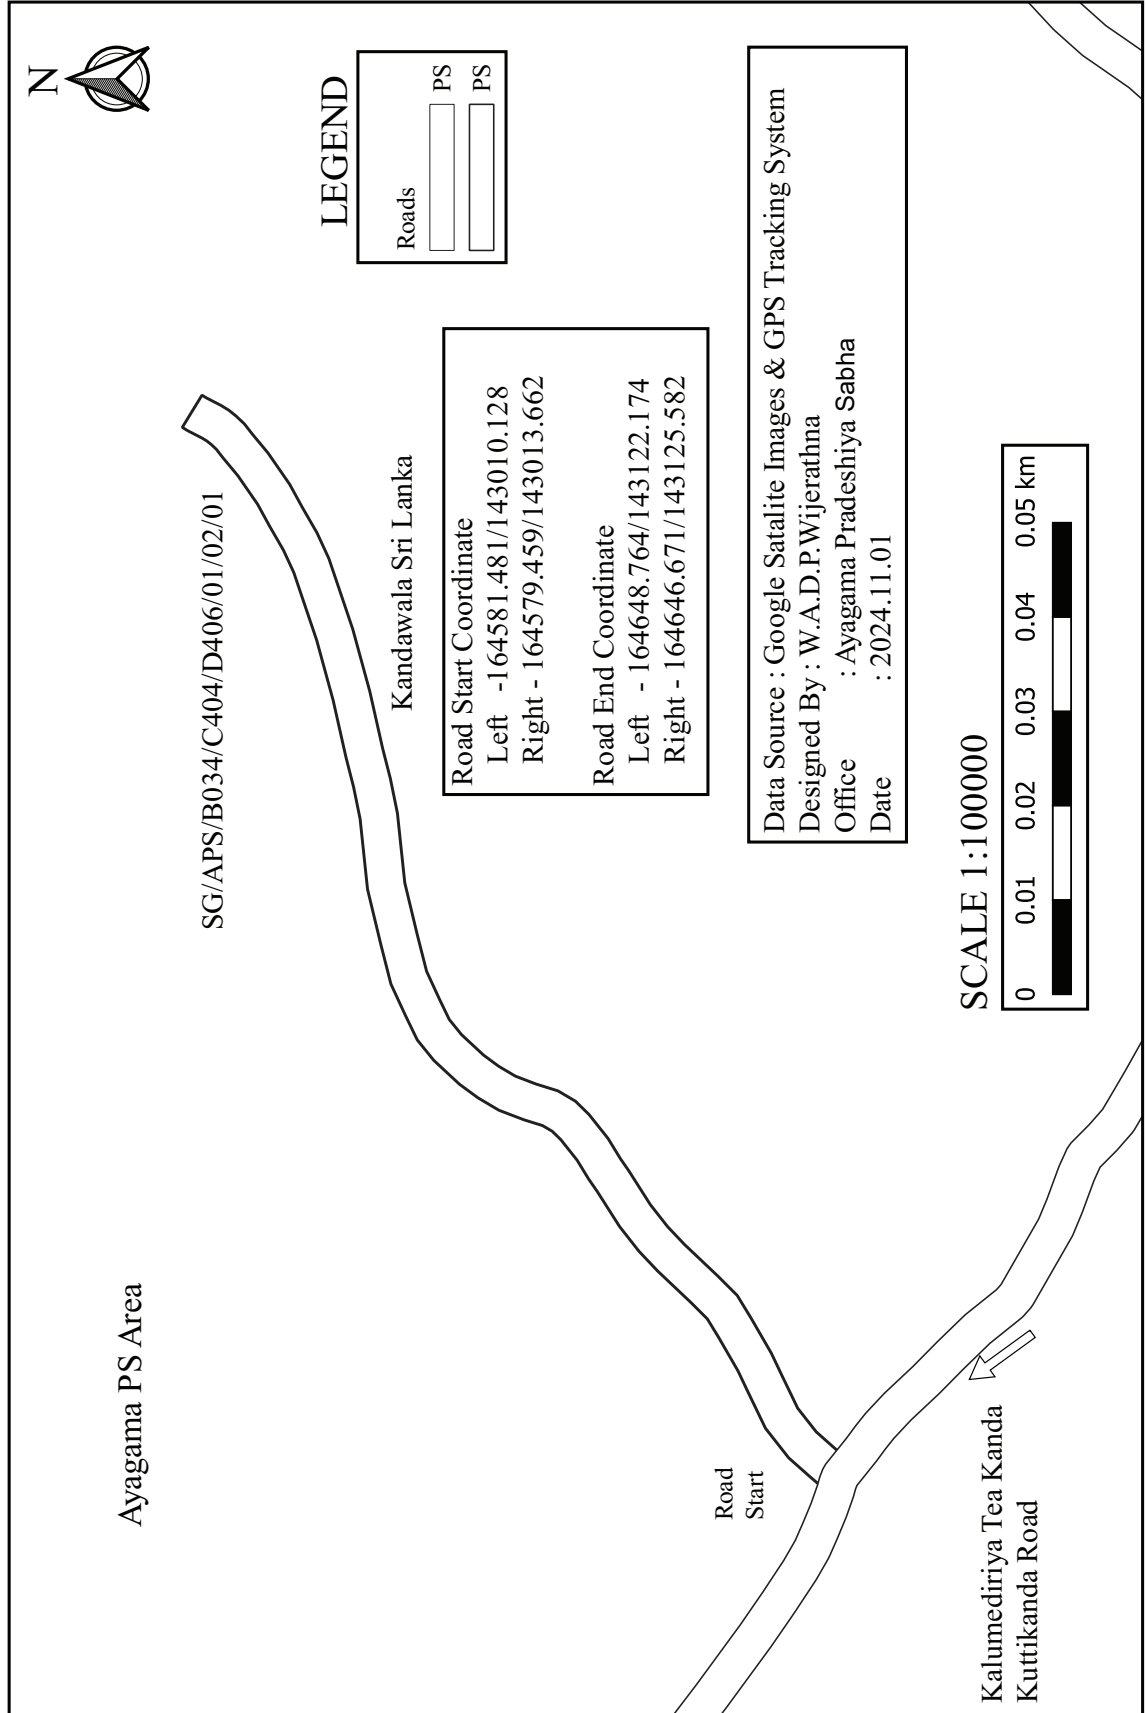


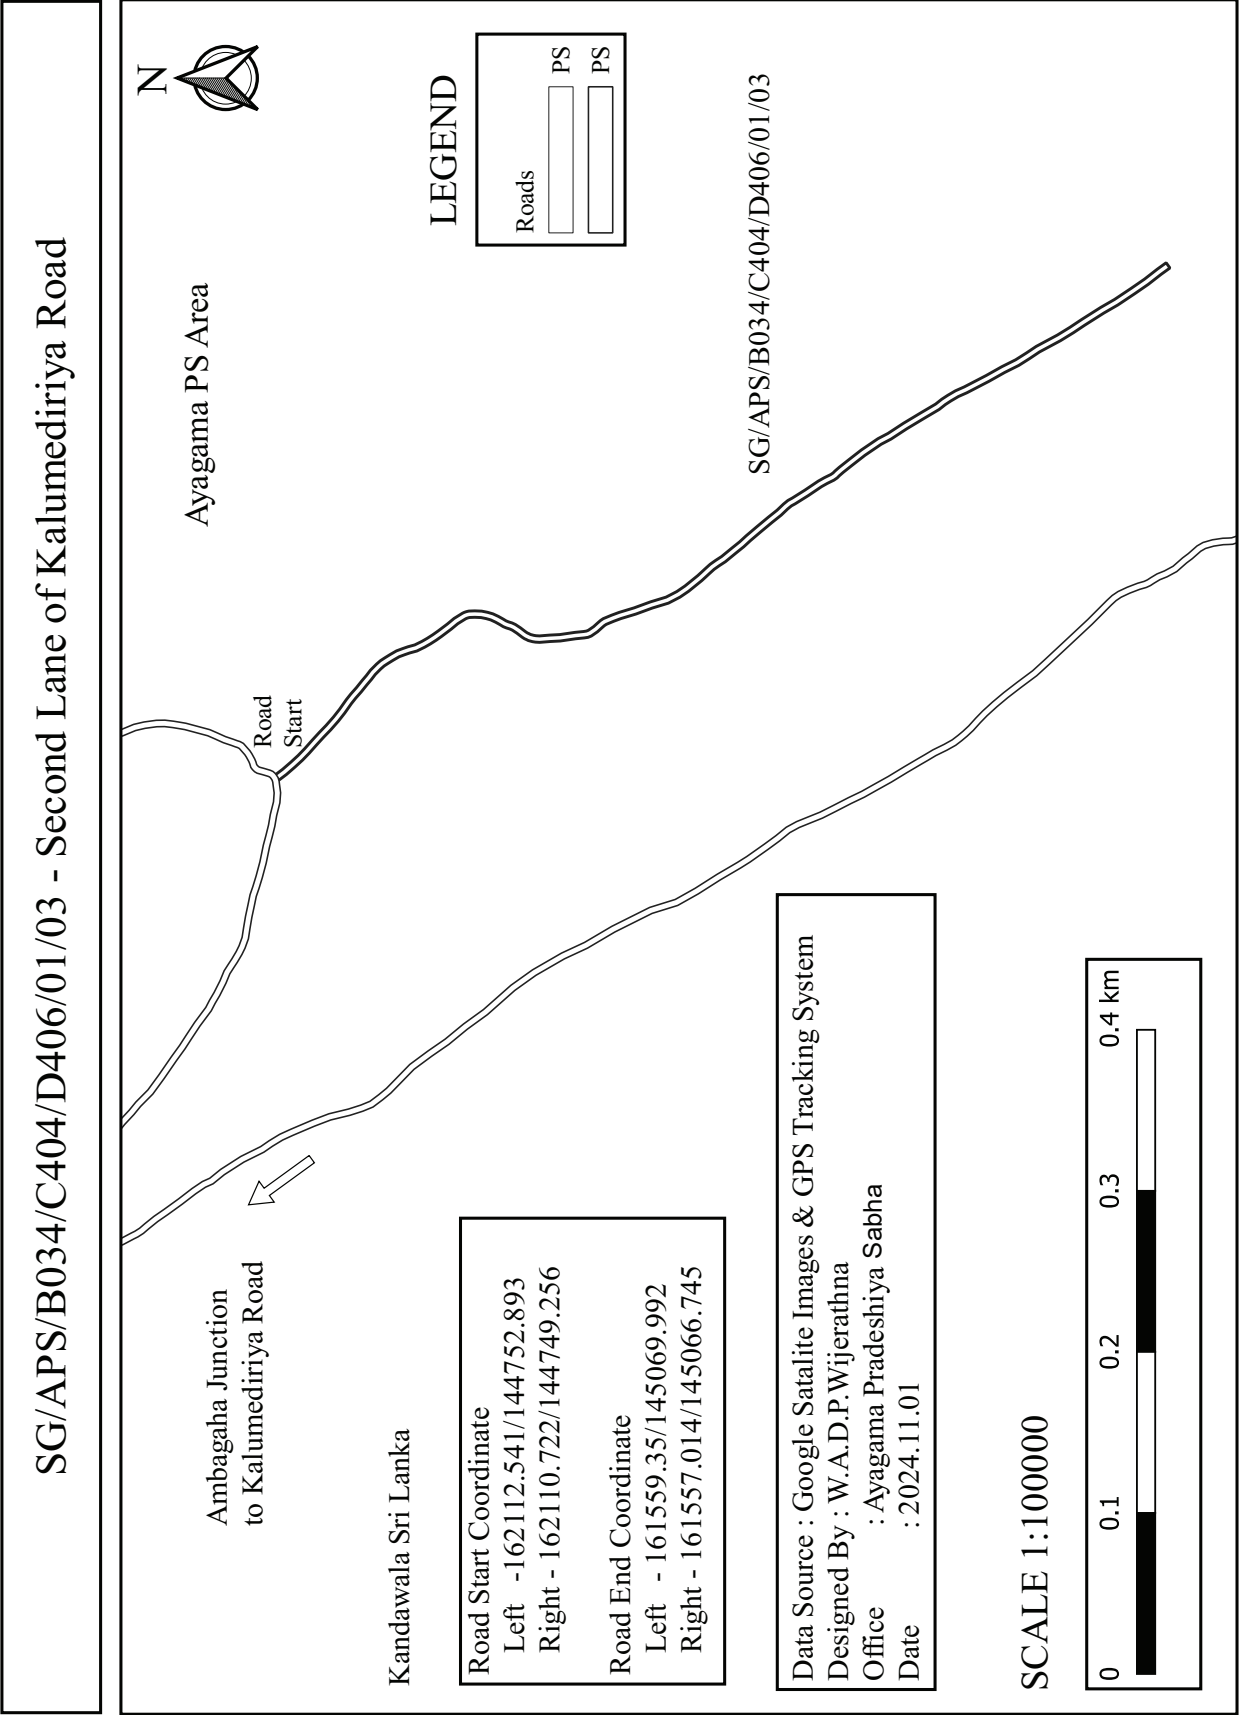


SG/APS/B034/C404/D406/01/04 - Third Lane of Kalumediya Road

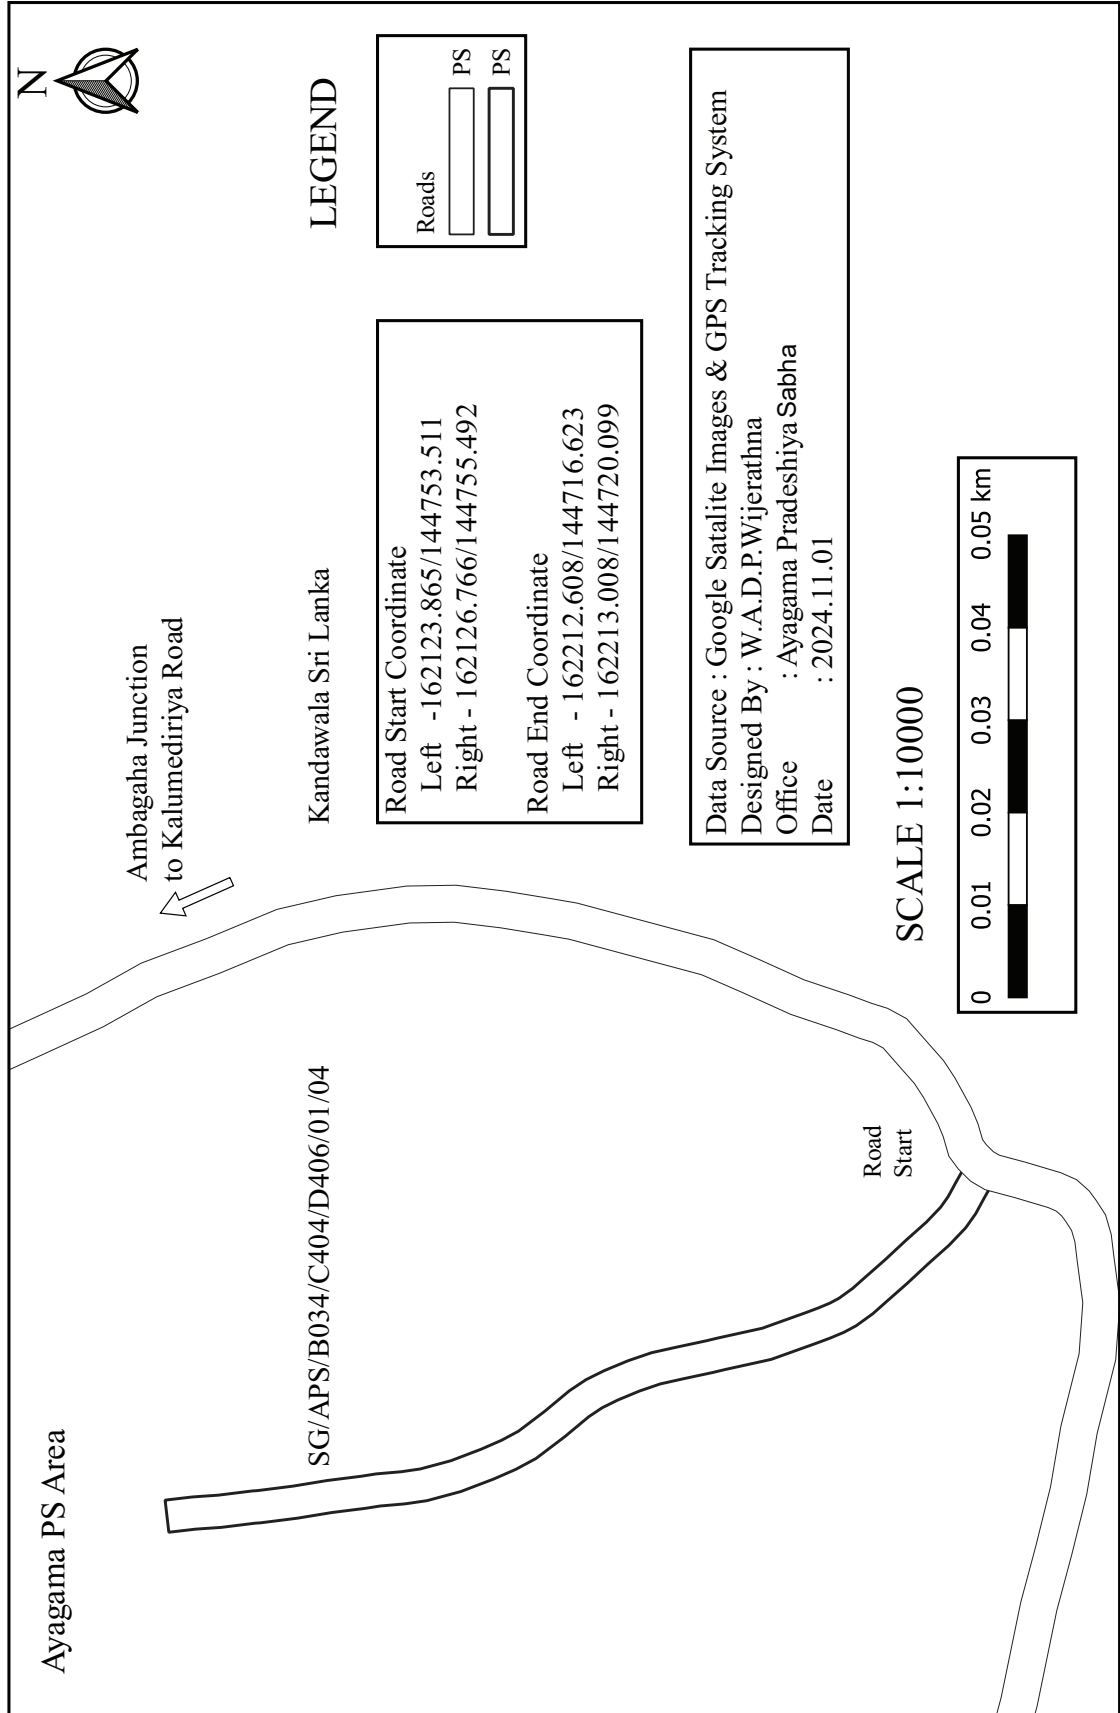


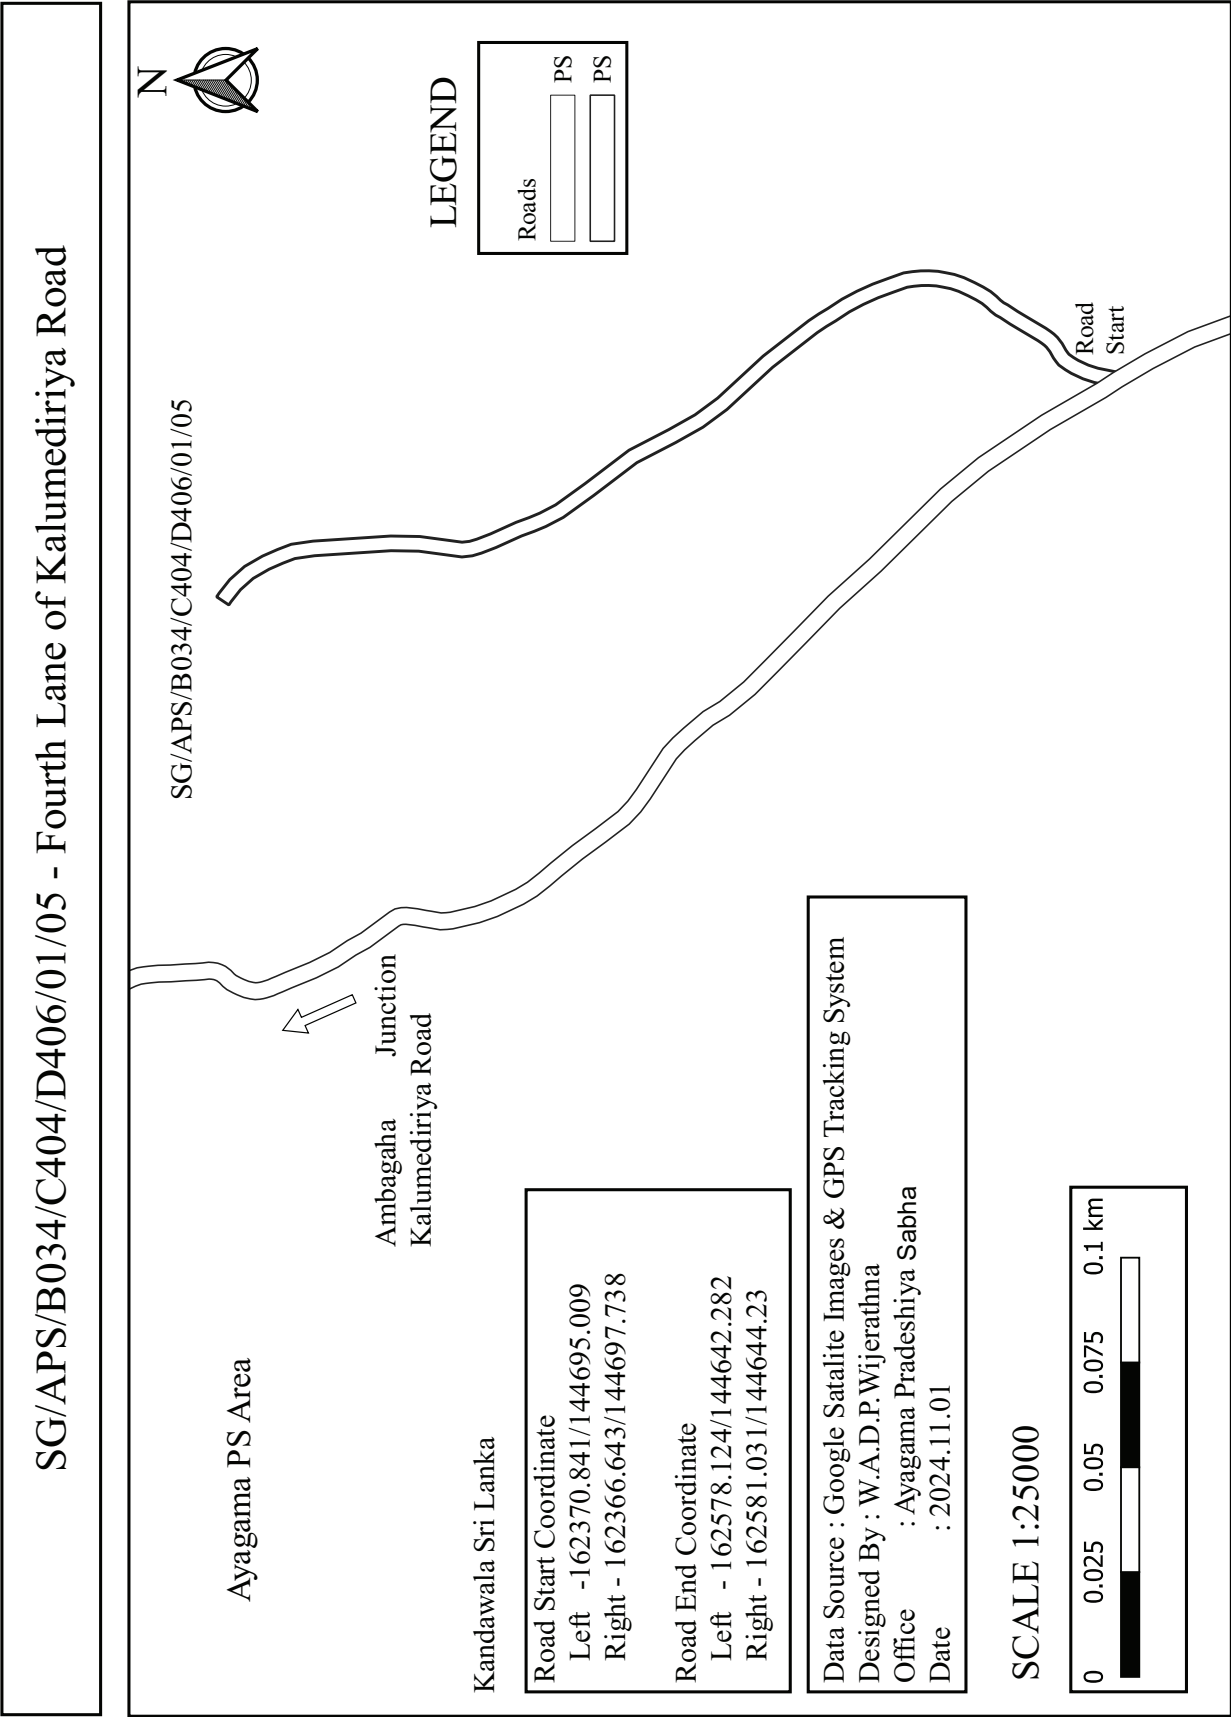


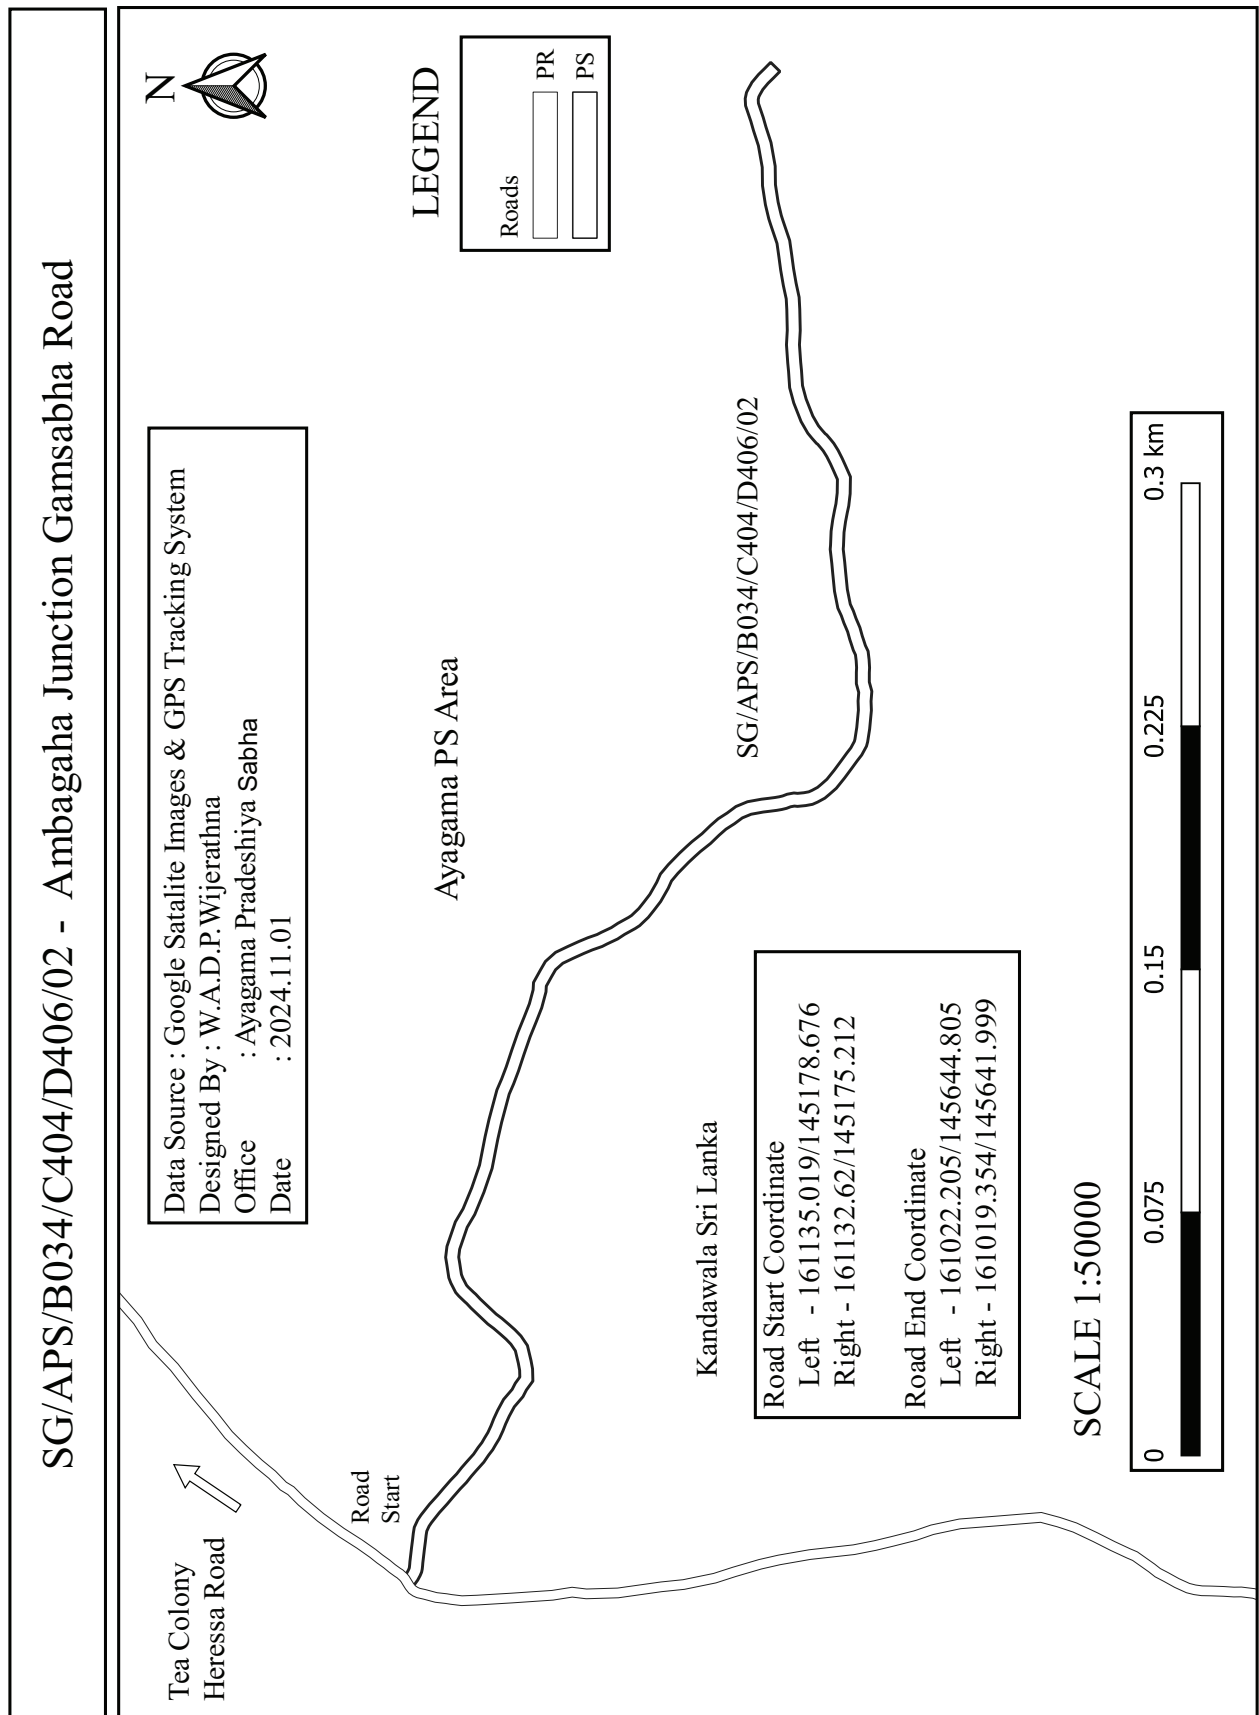


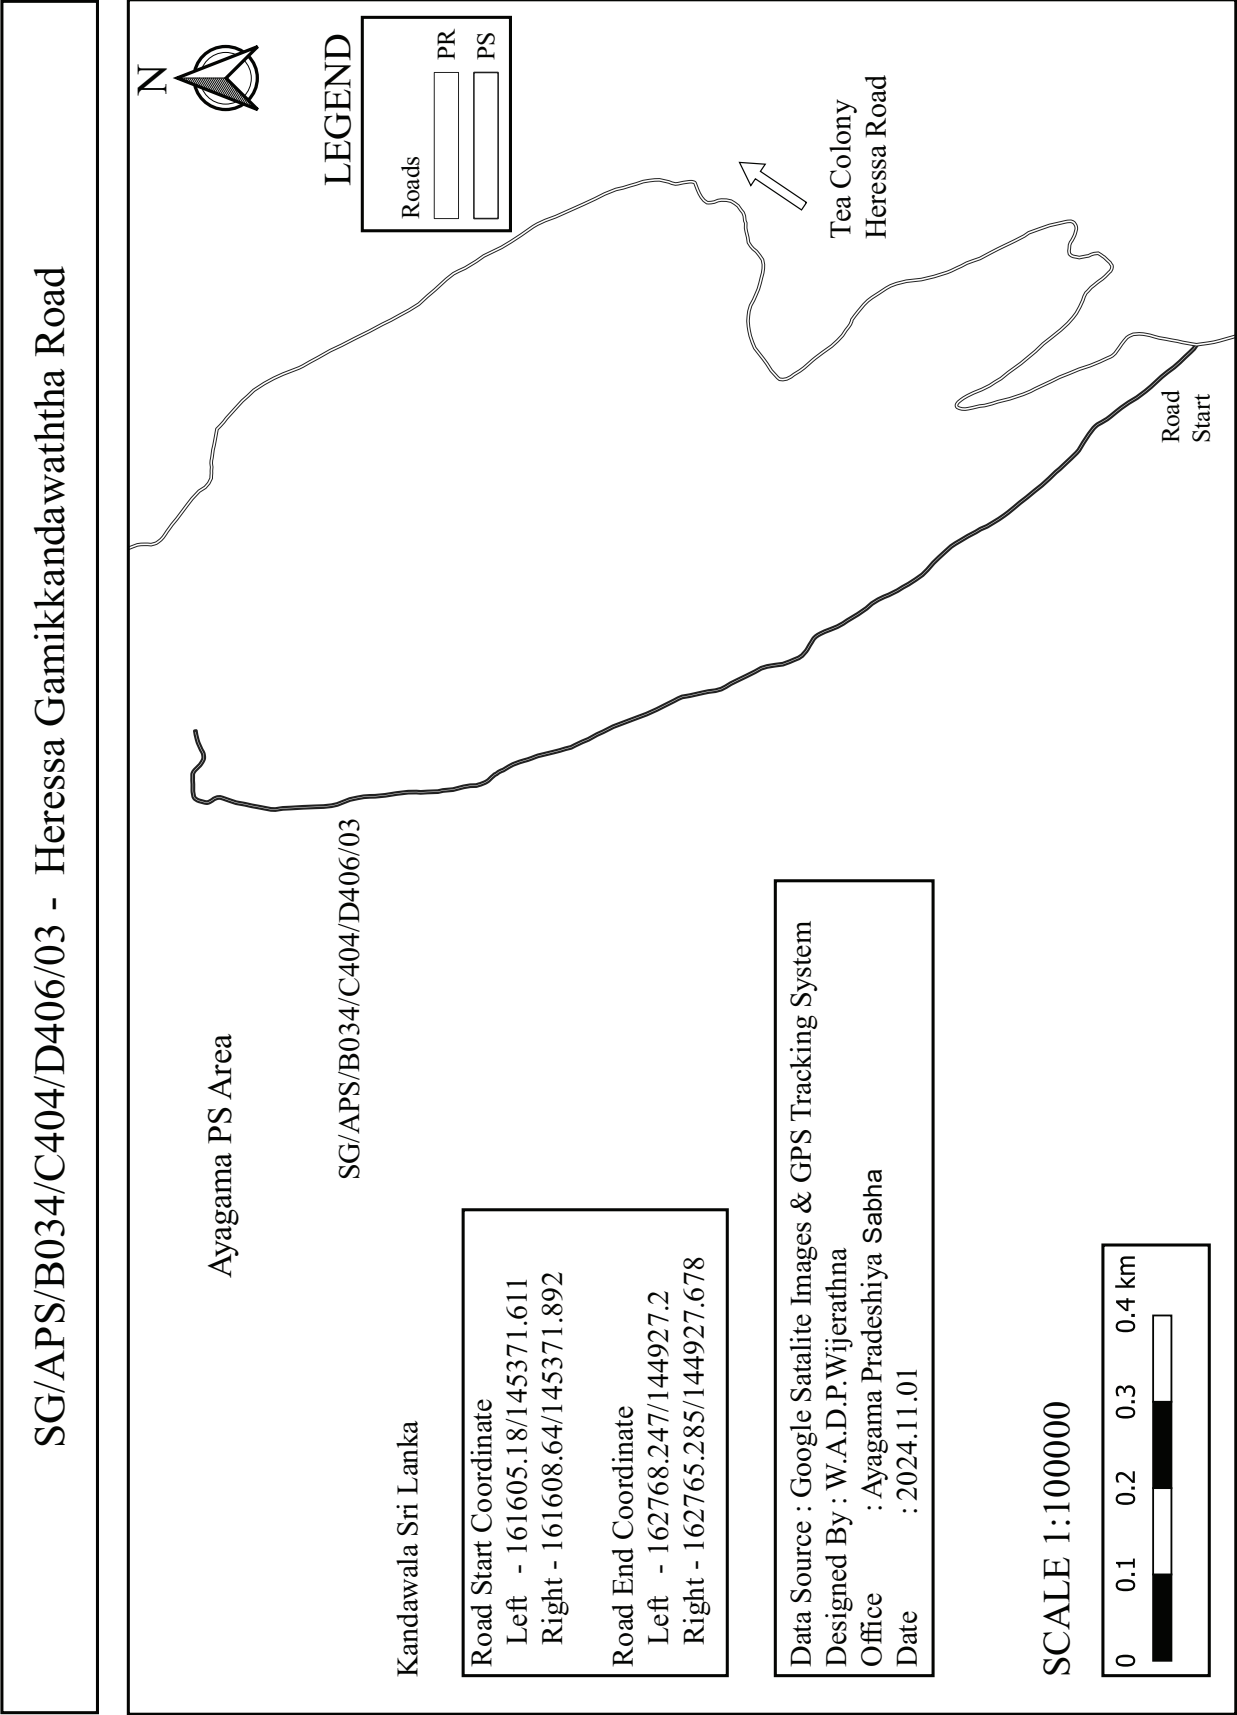



SG/APS/B034/C404/D406/03/01 - First Lane of Heressa Gamikkandawaththa Road

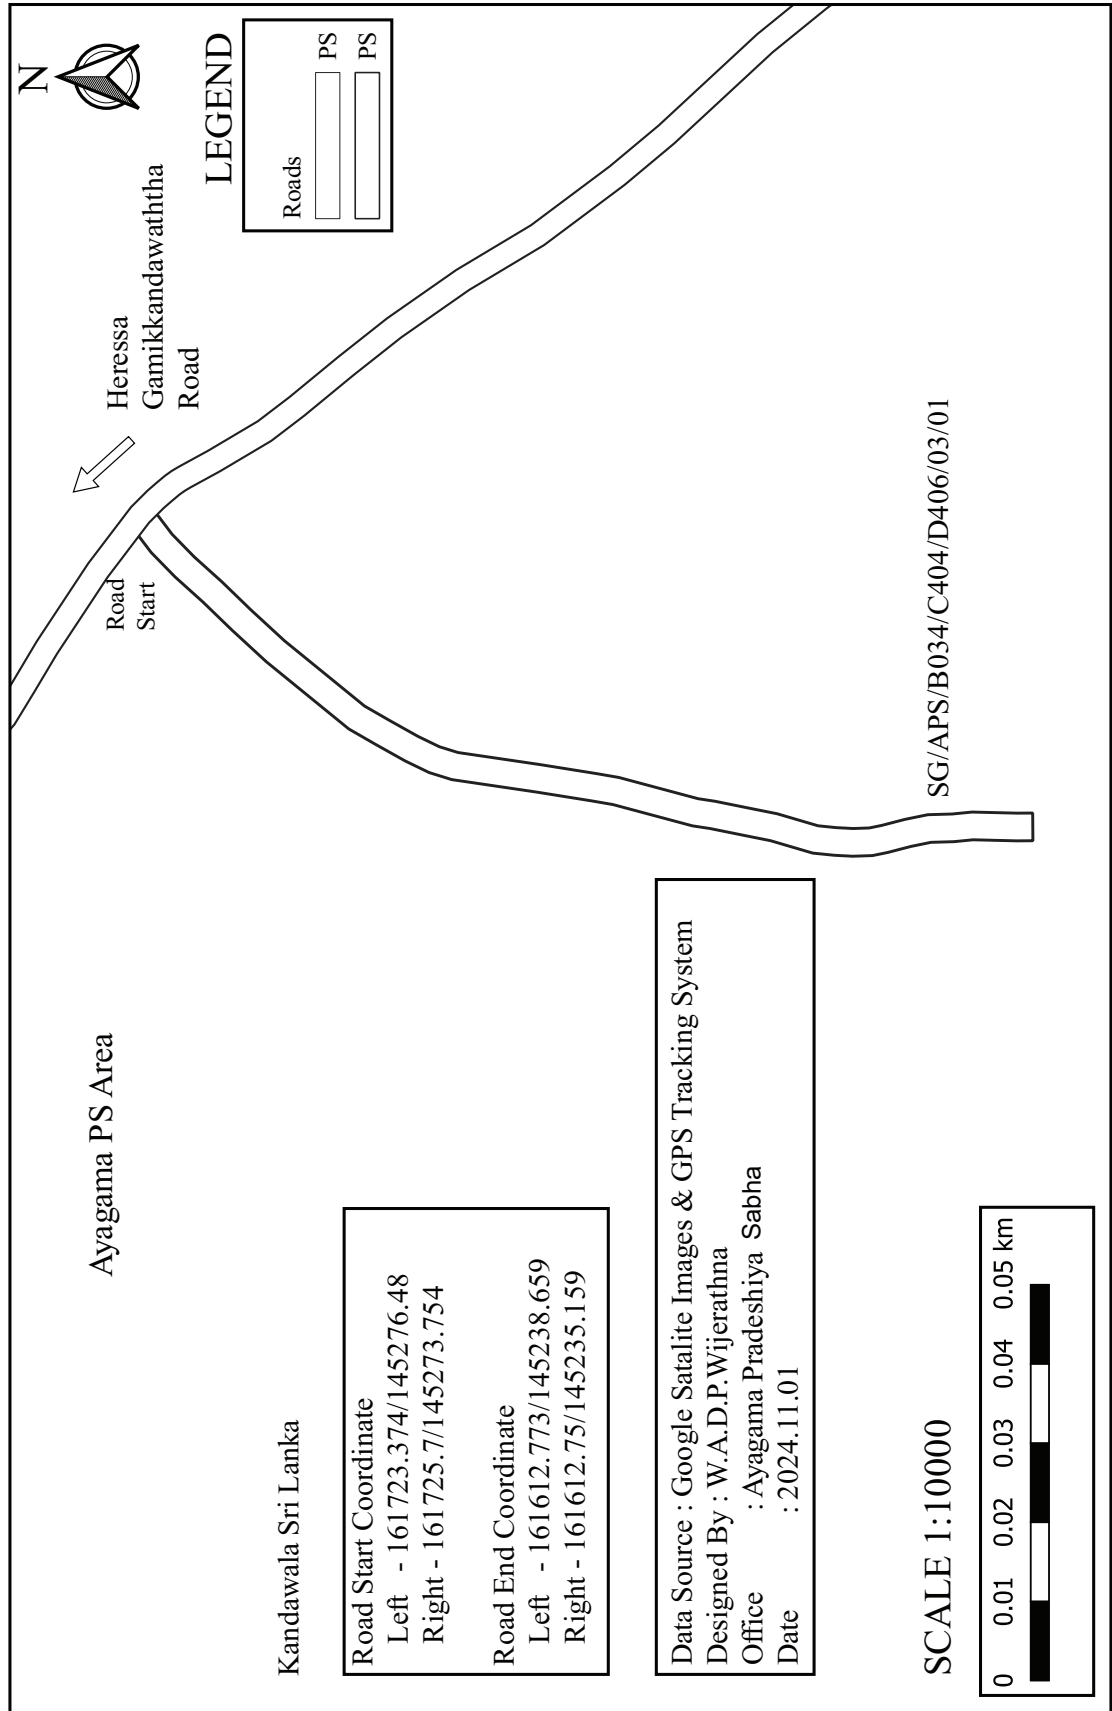


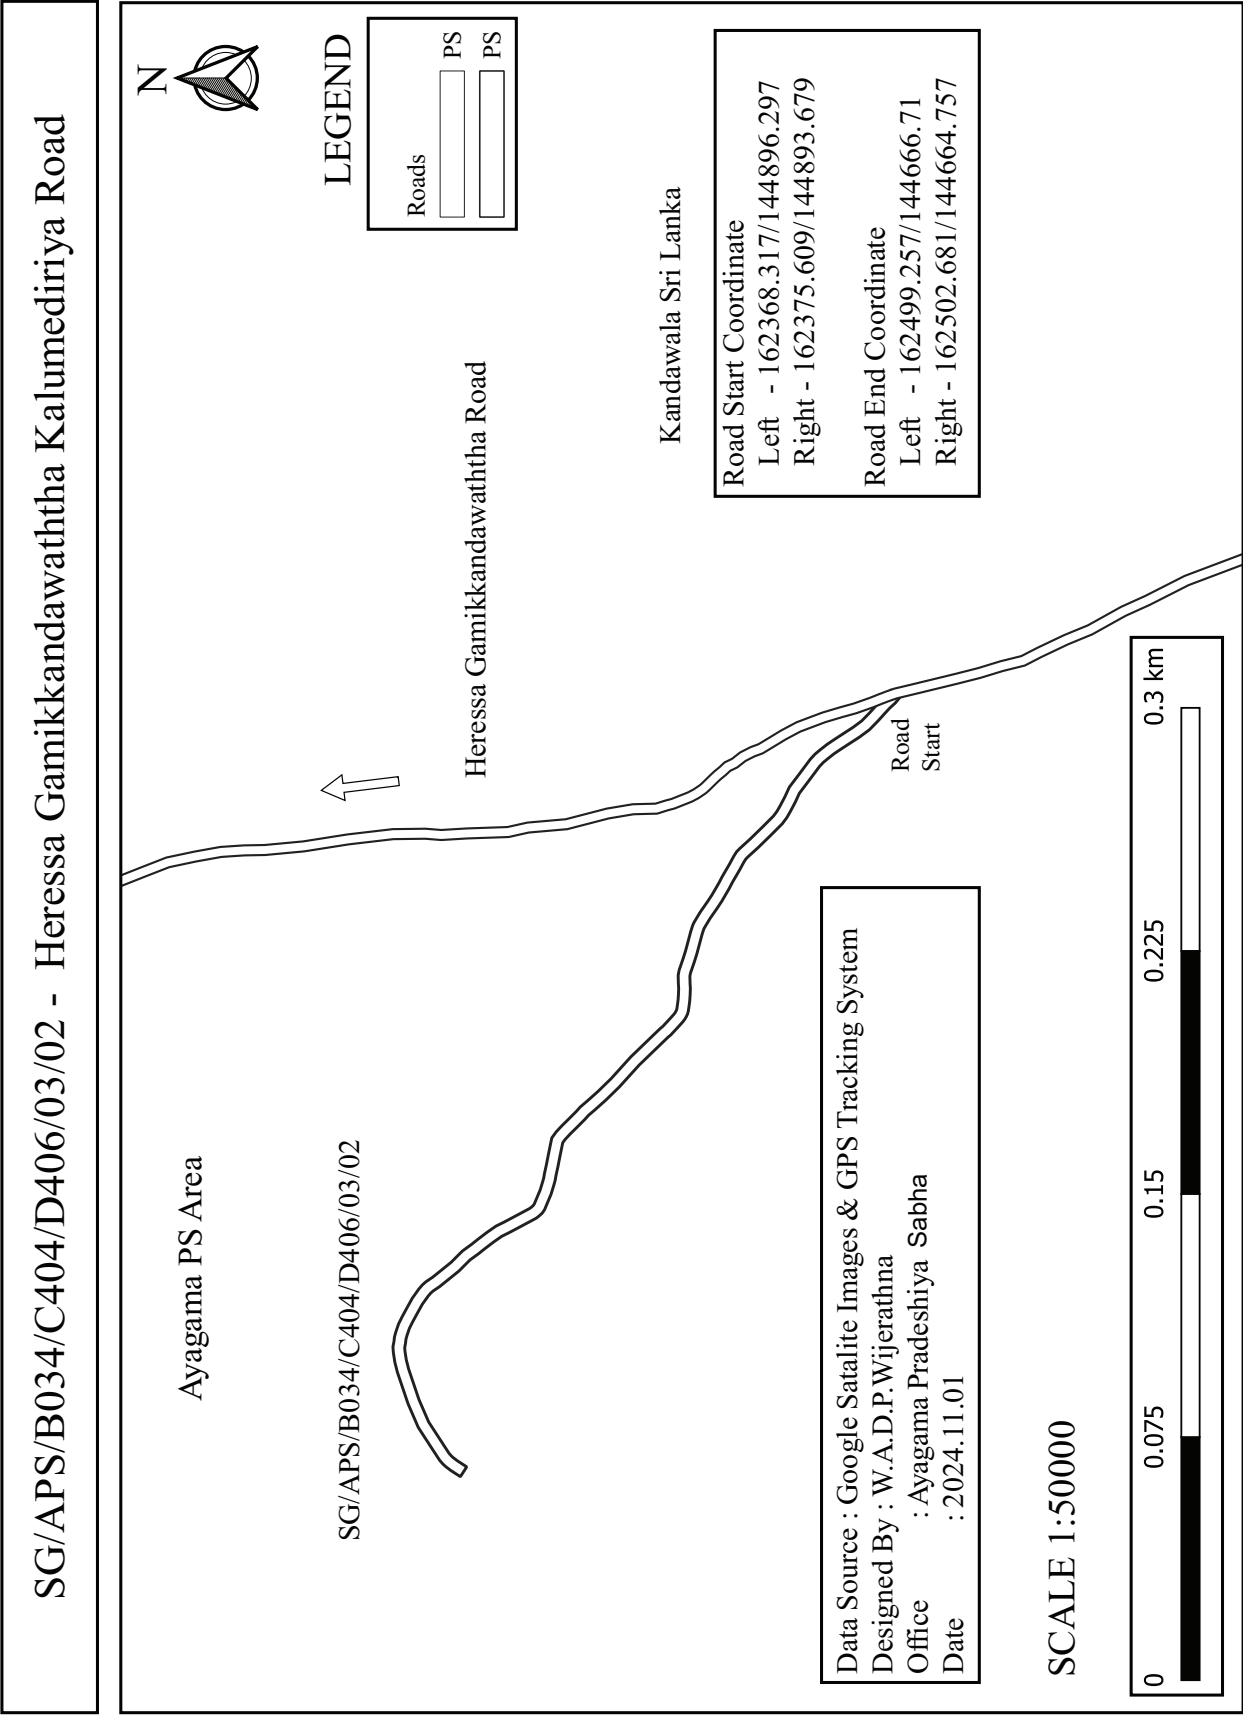


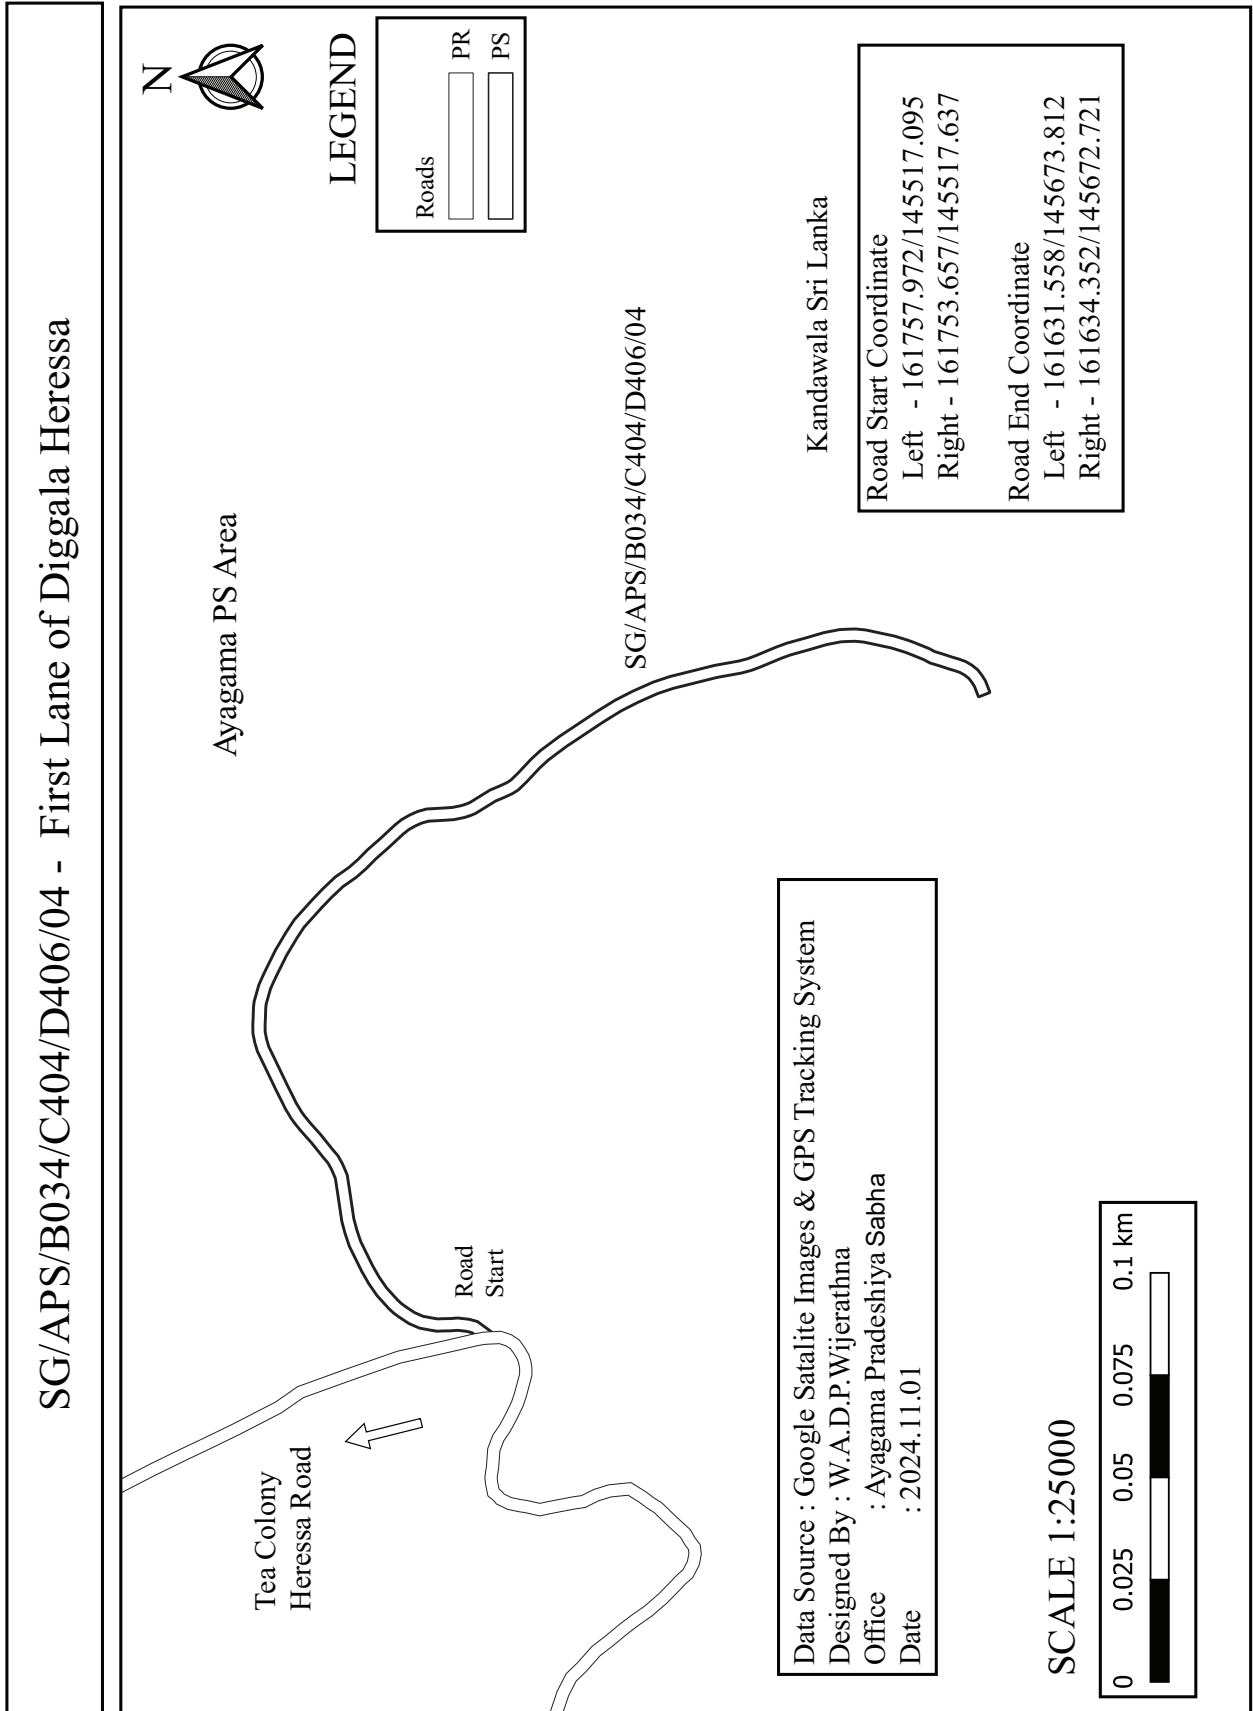


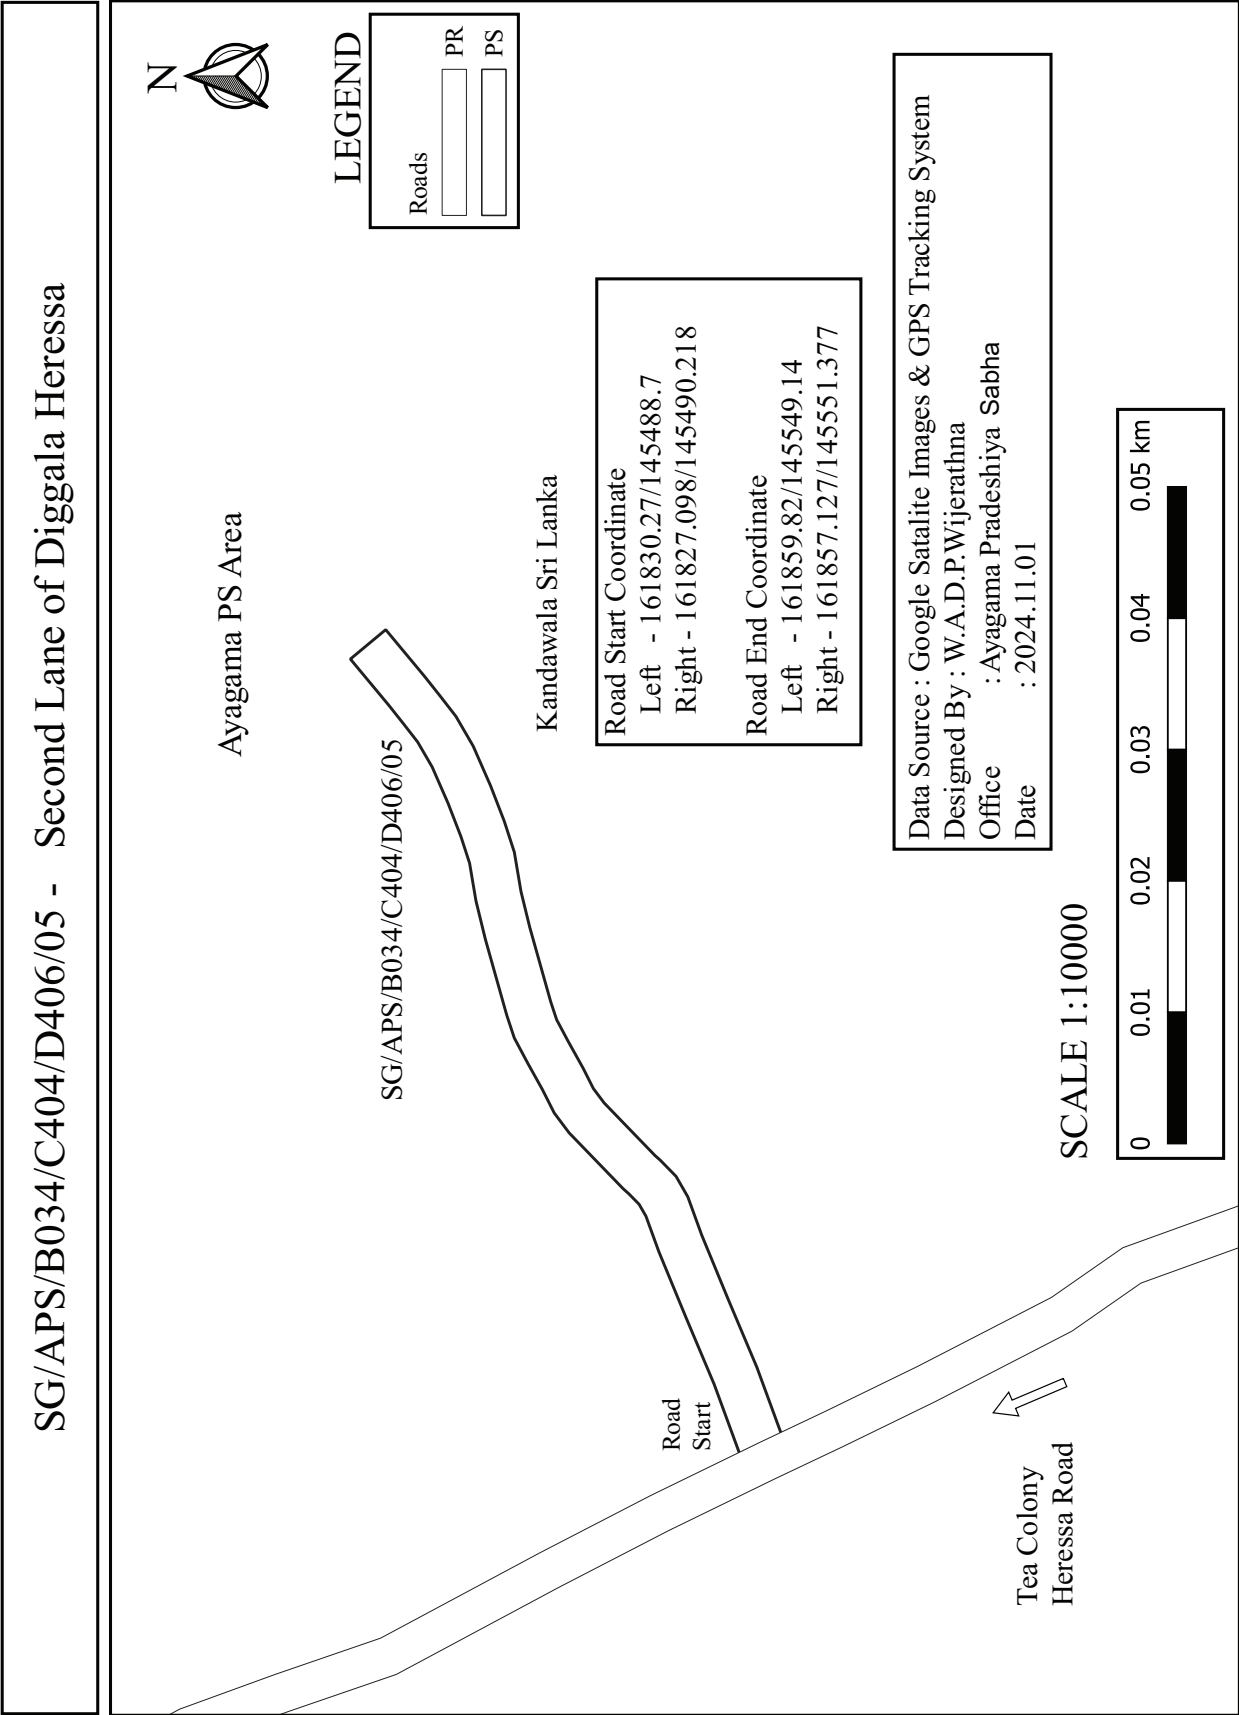

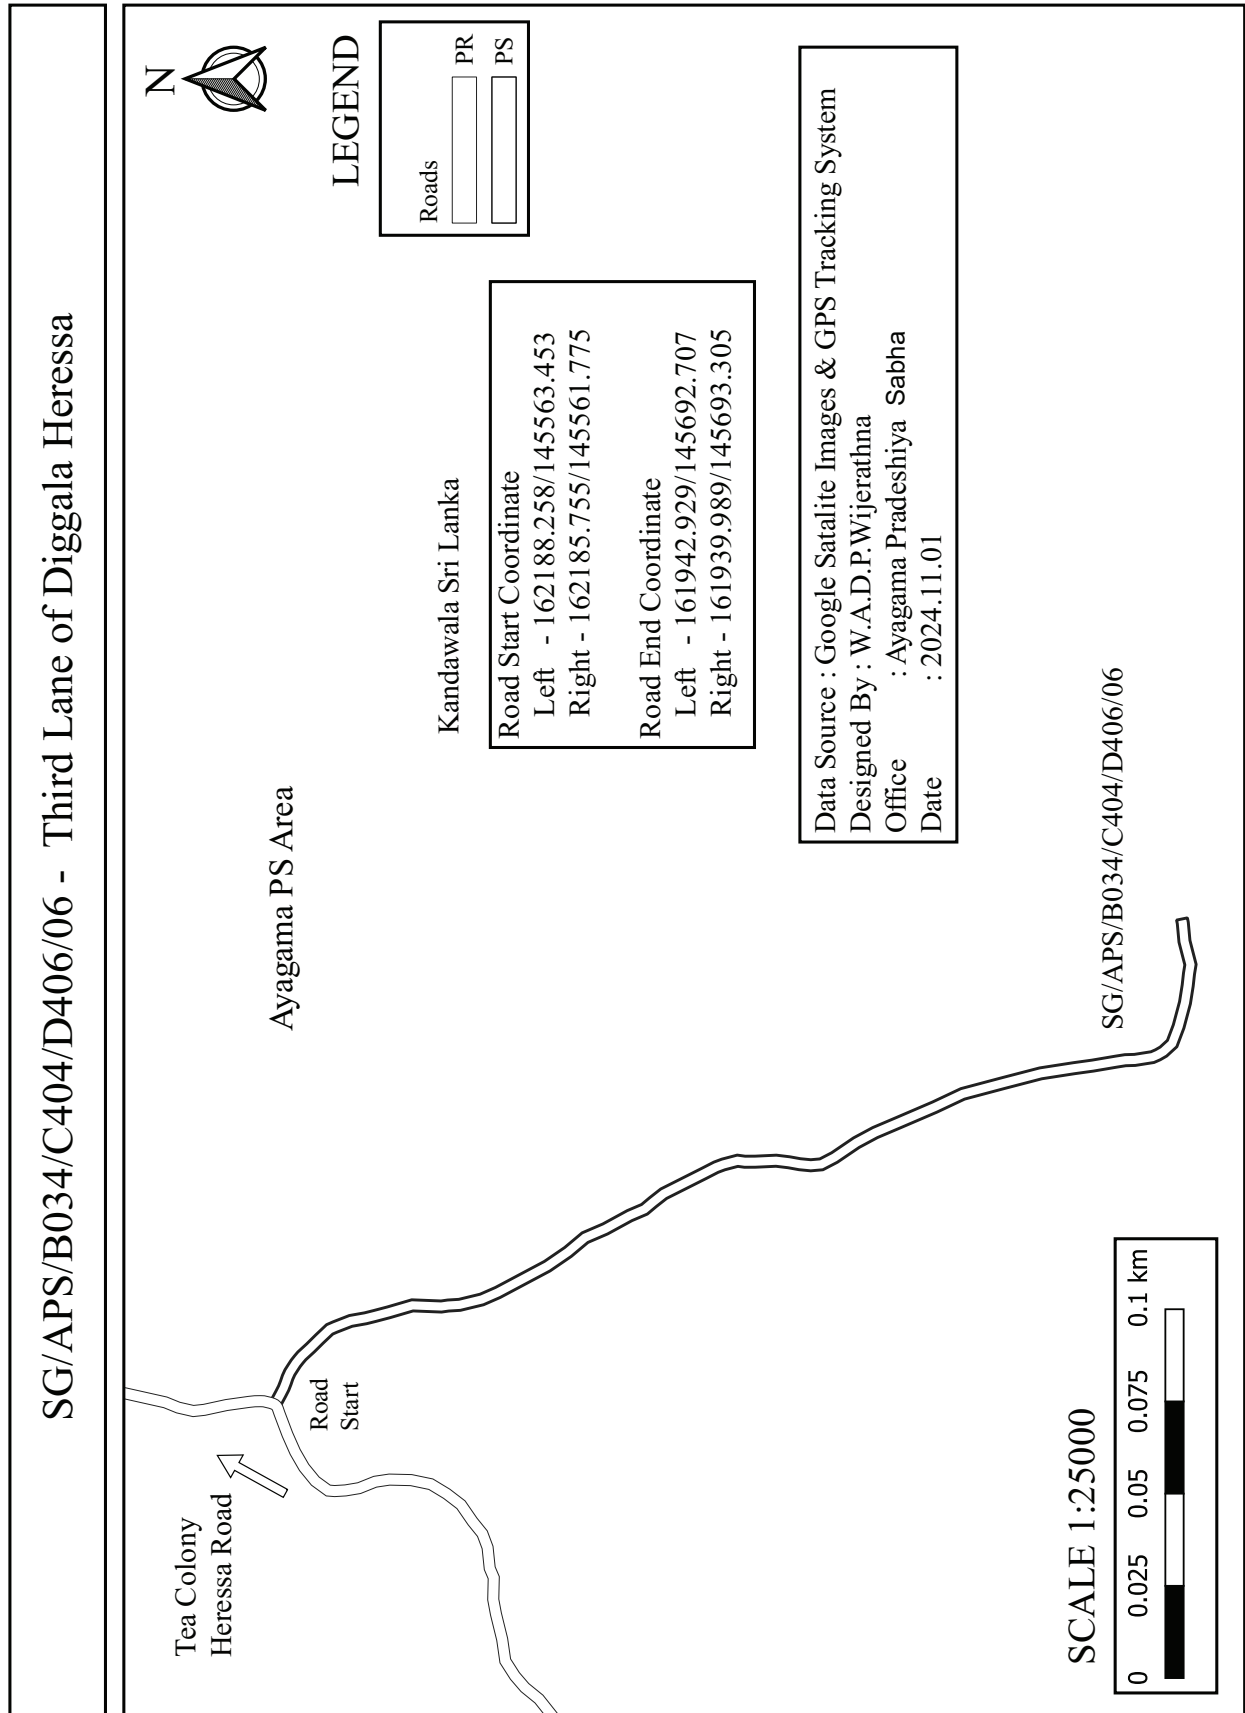


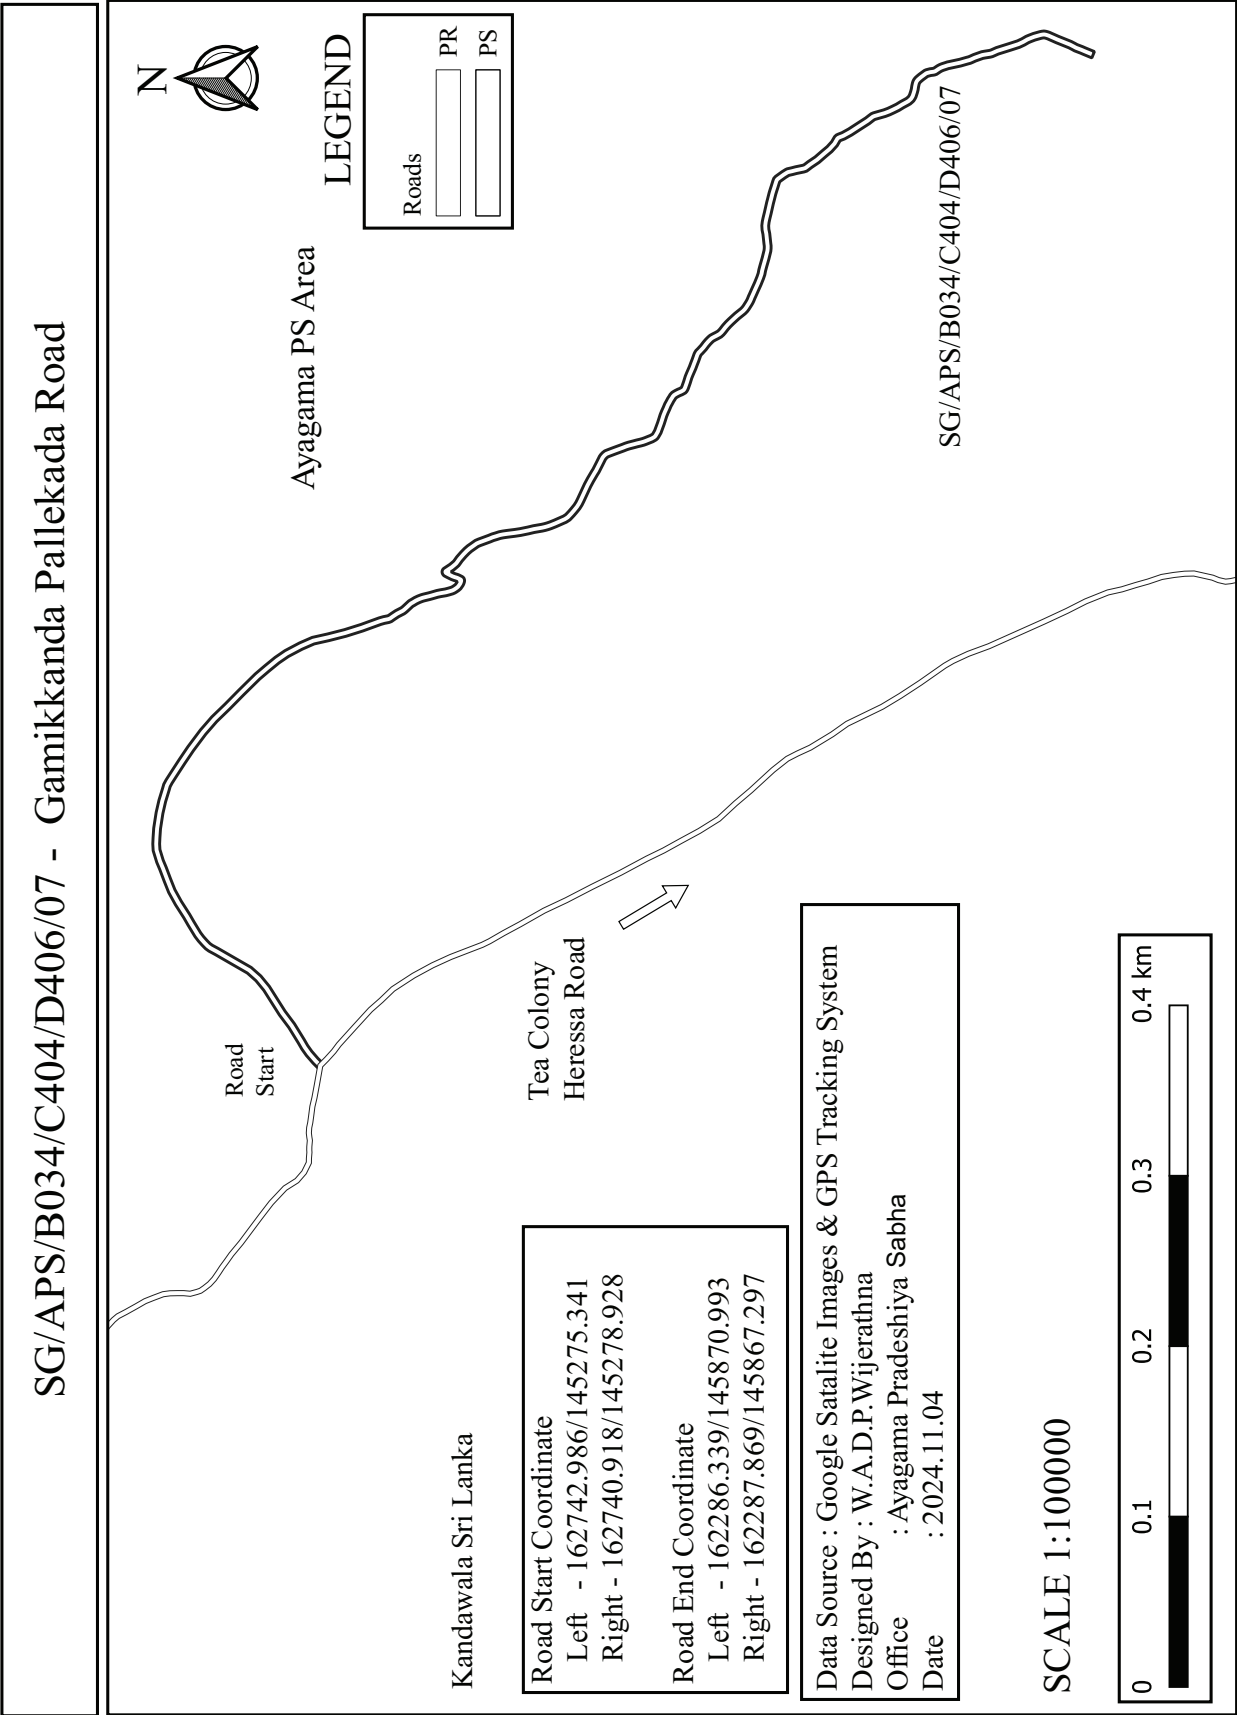


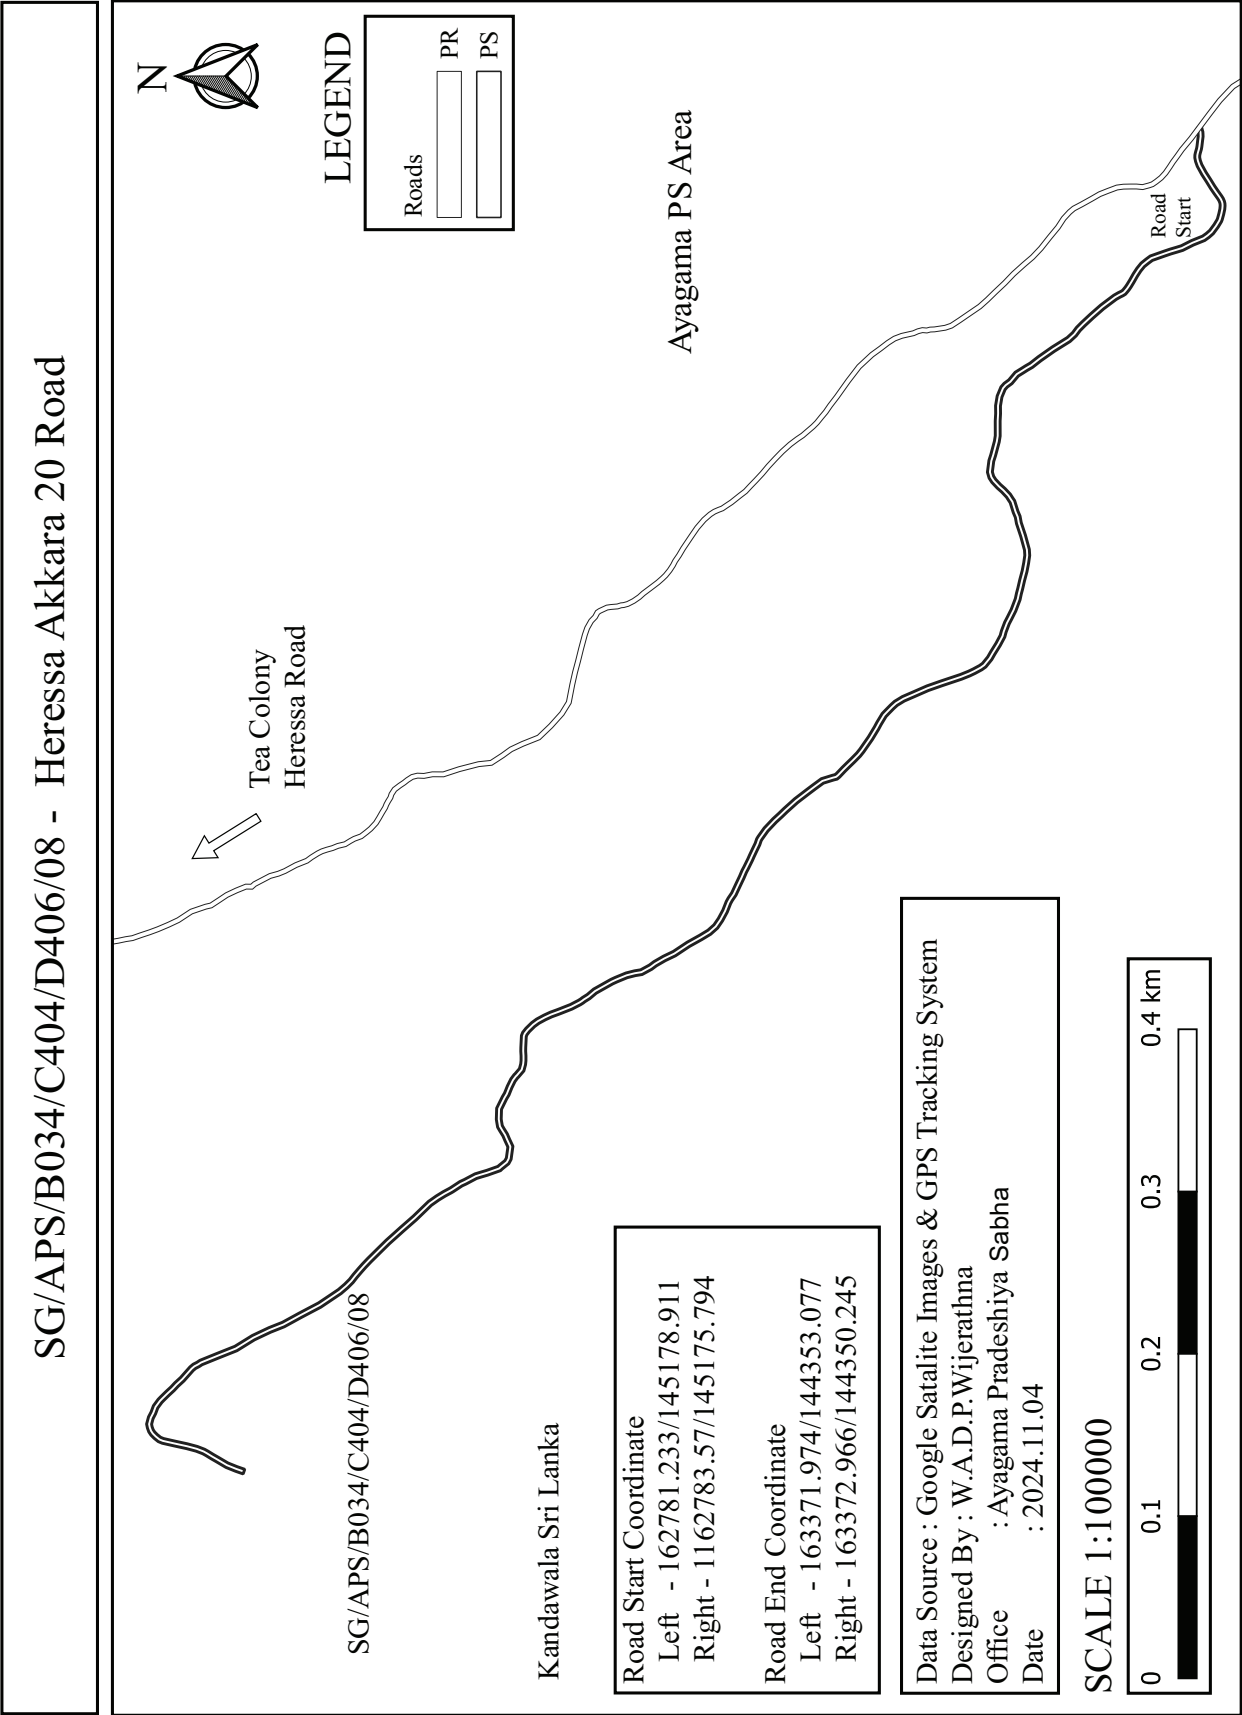


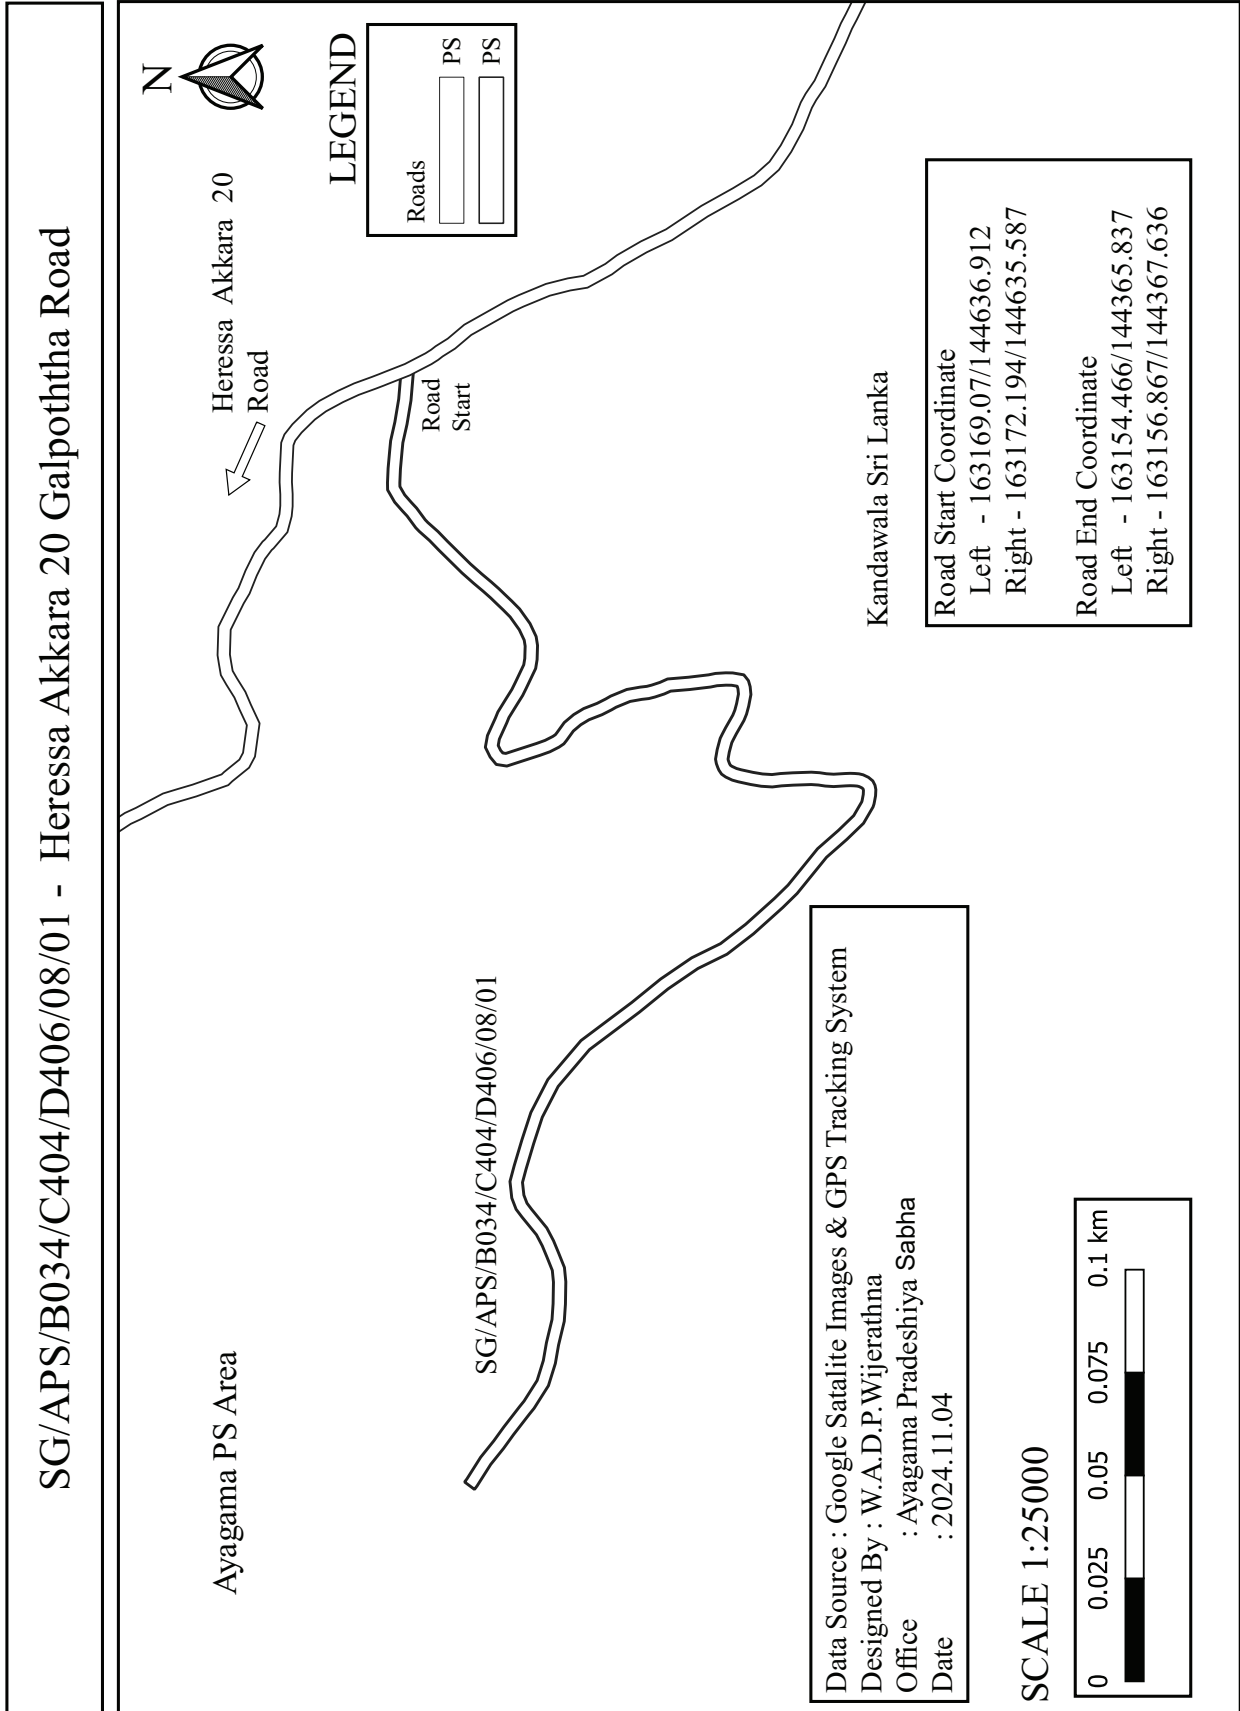





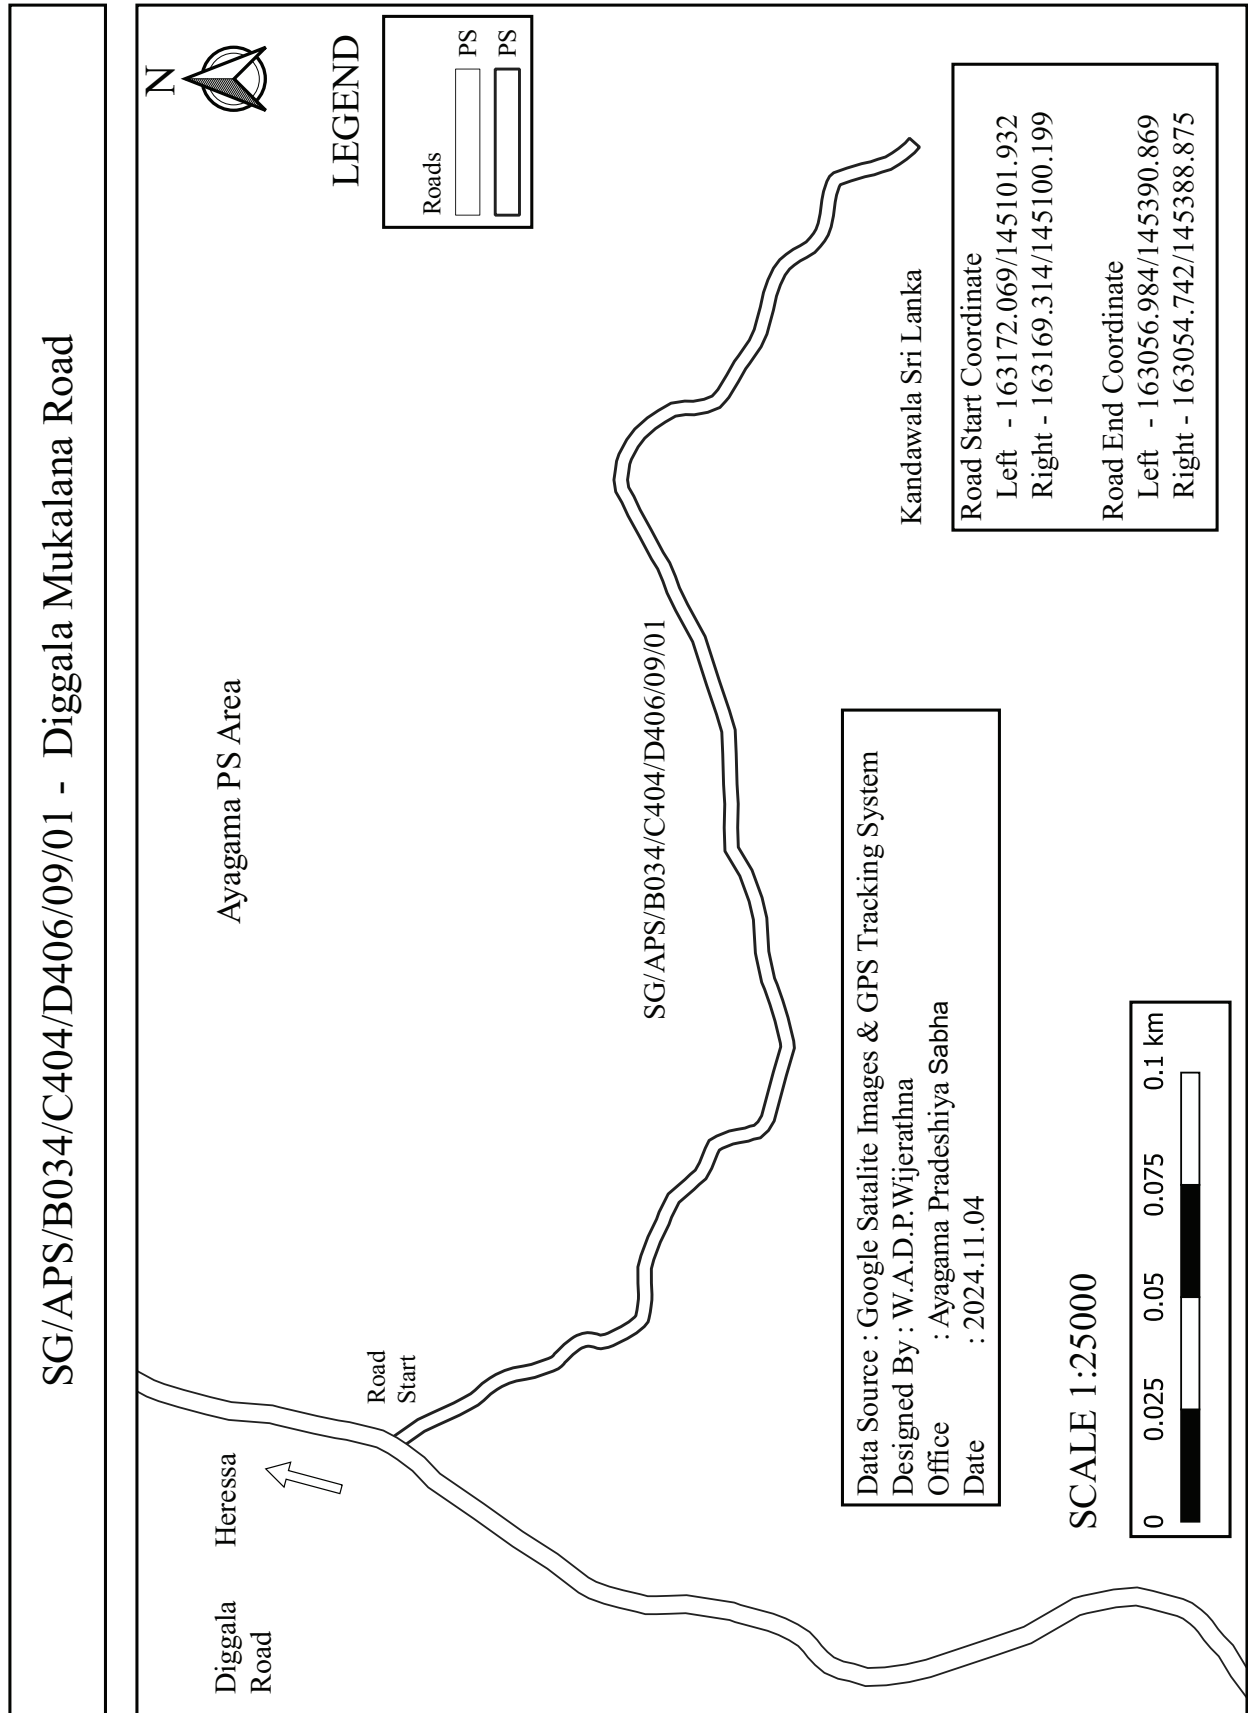


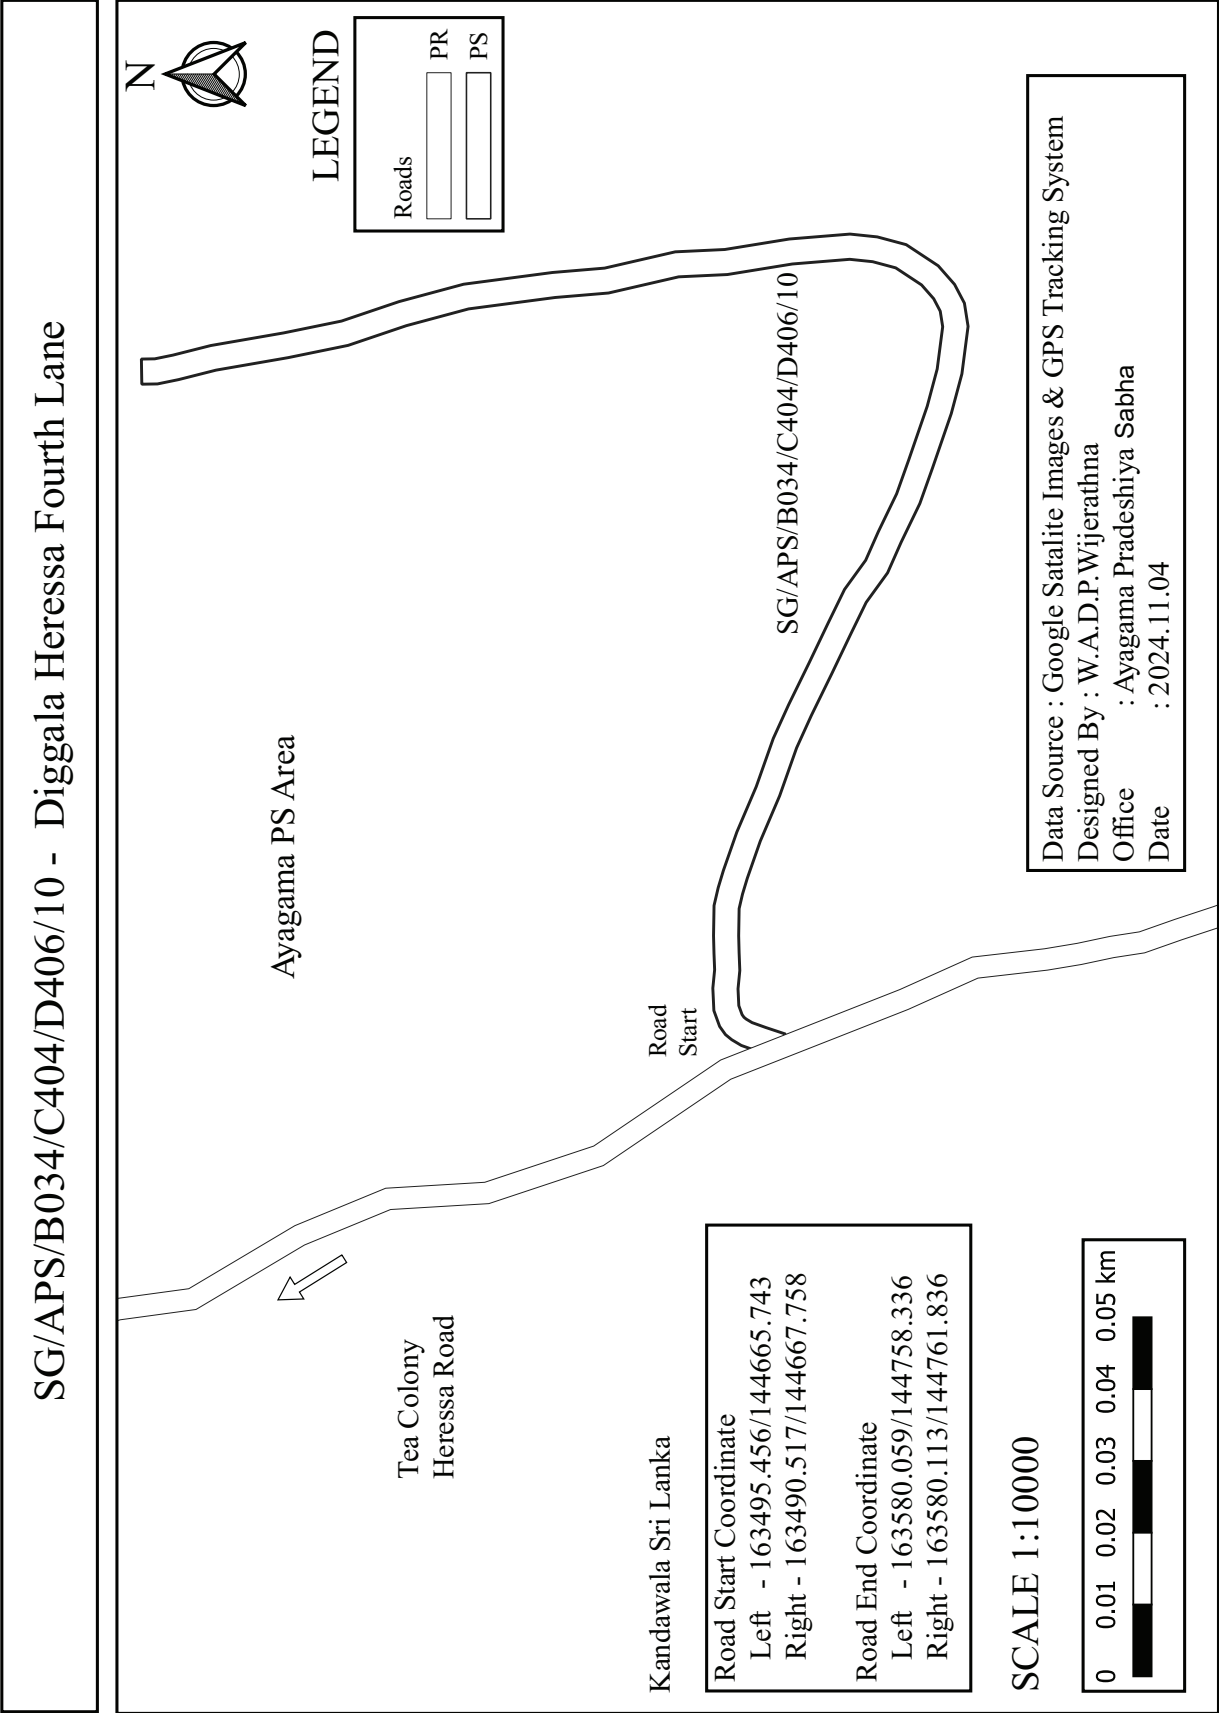

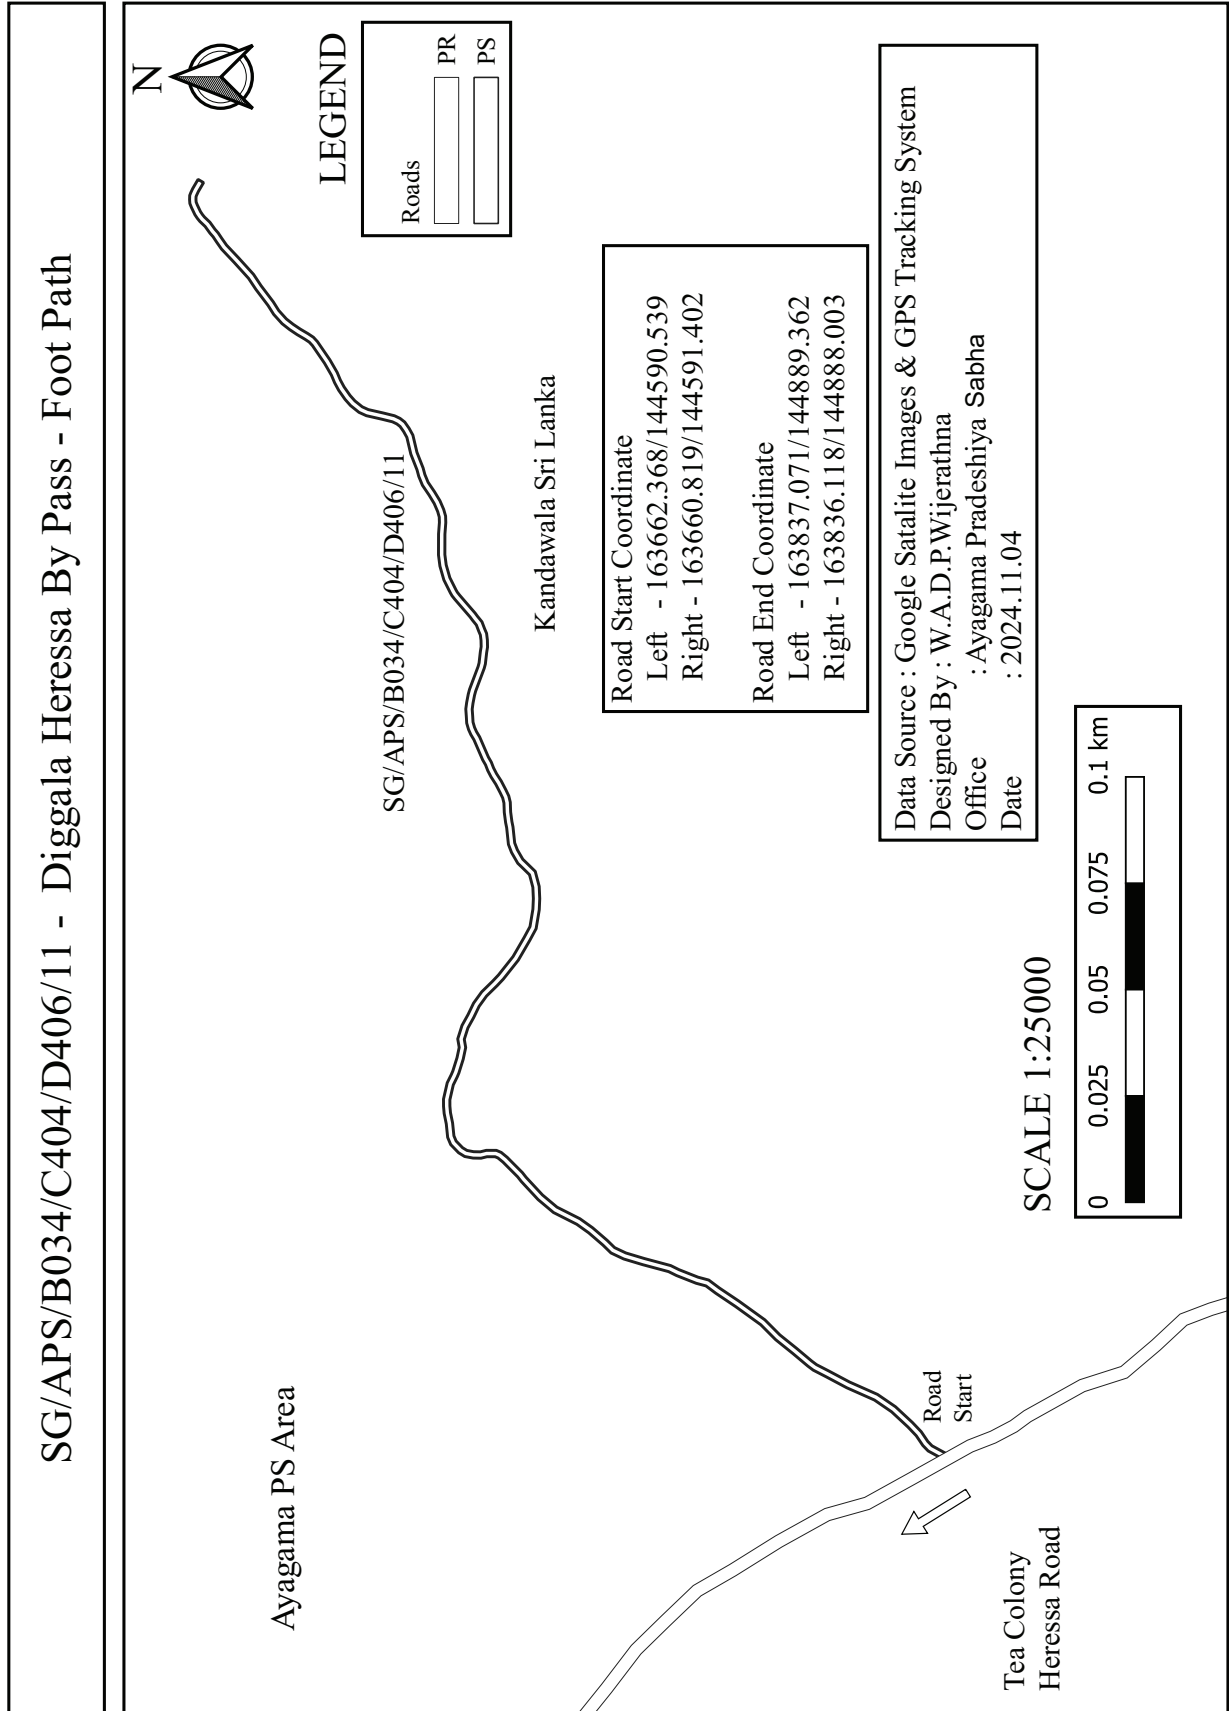


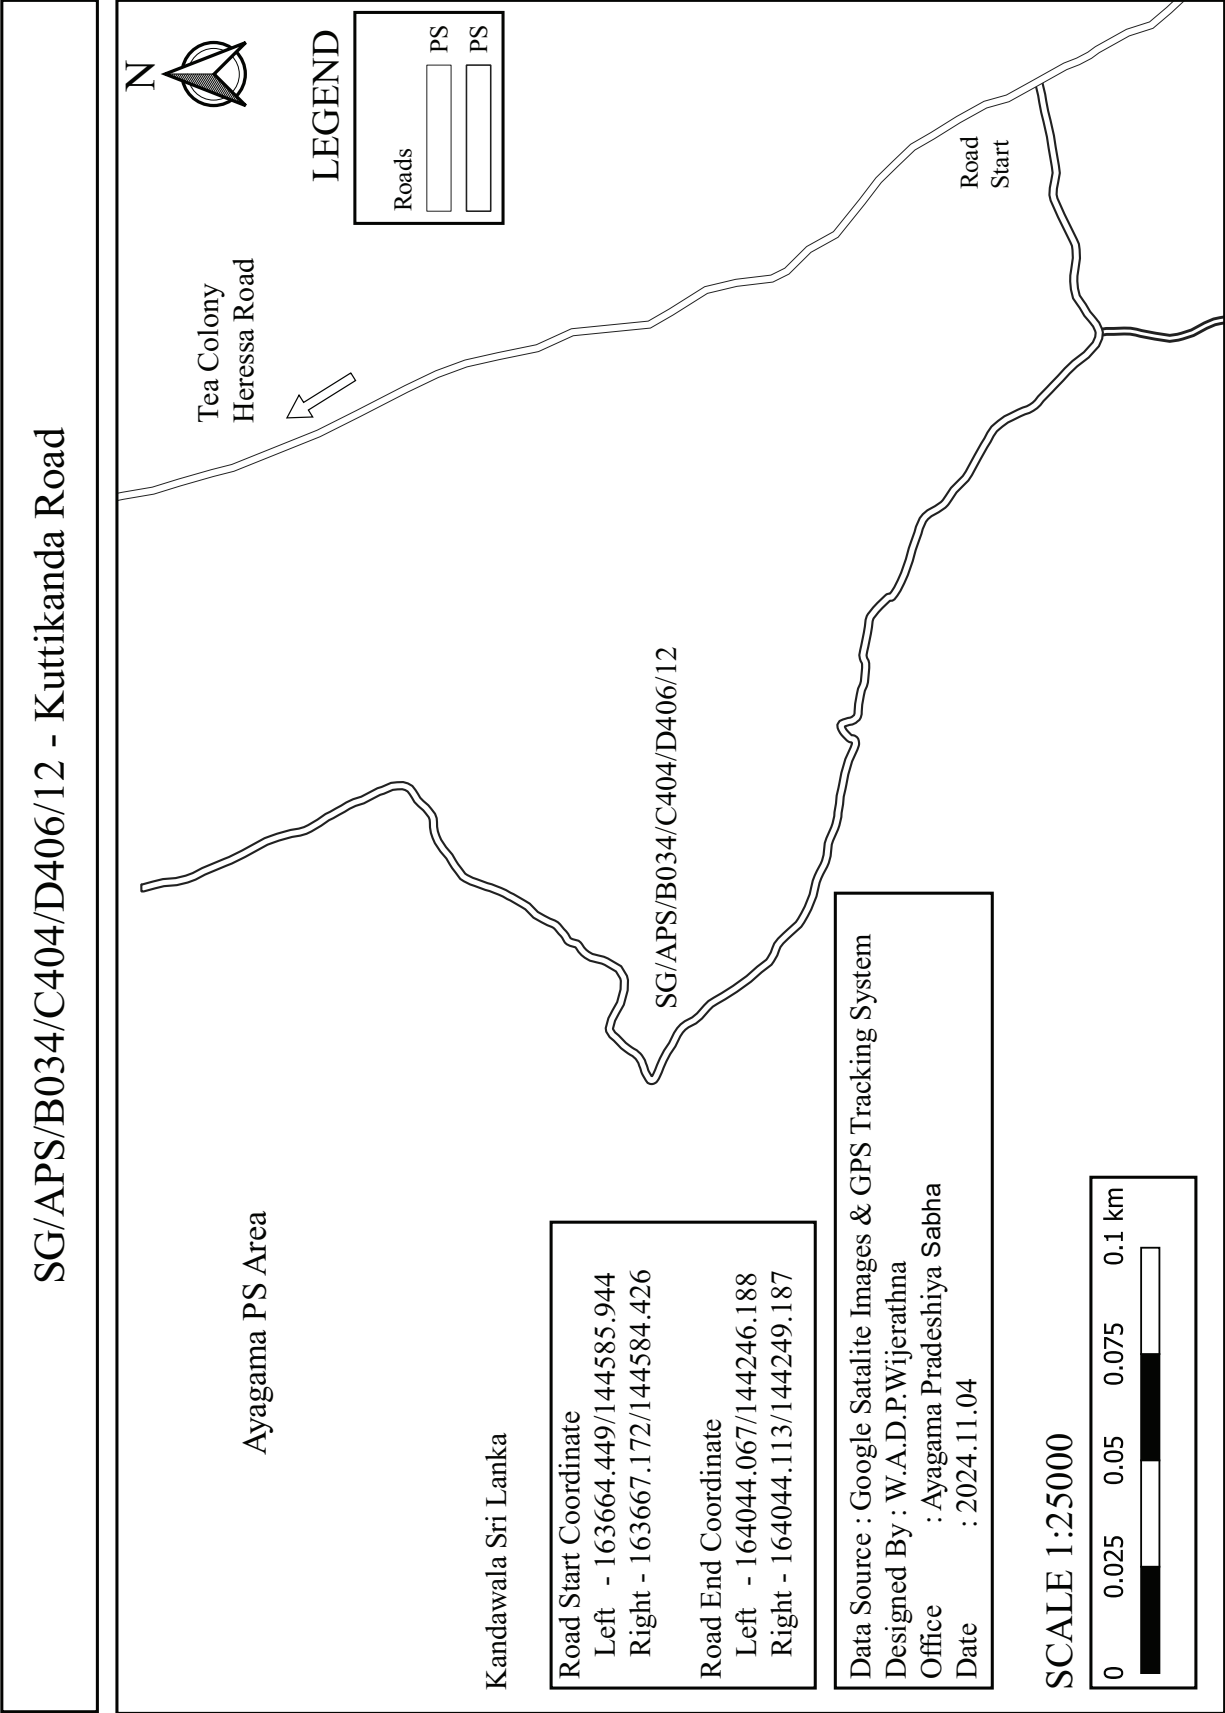


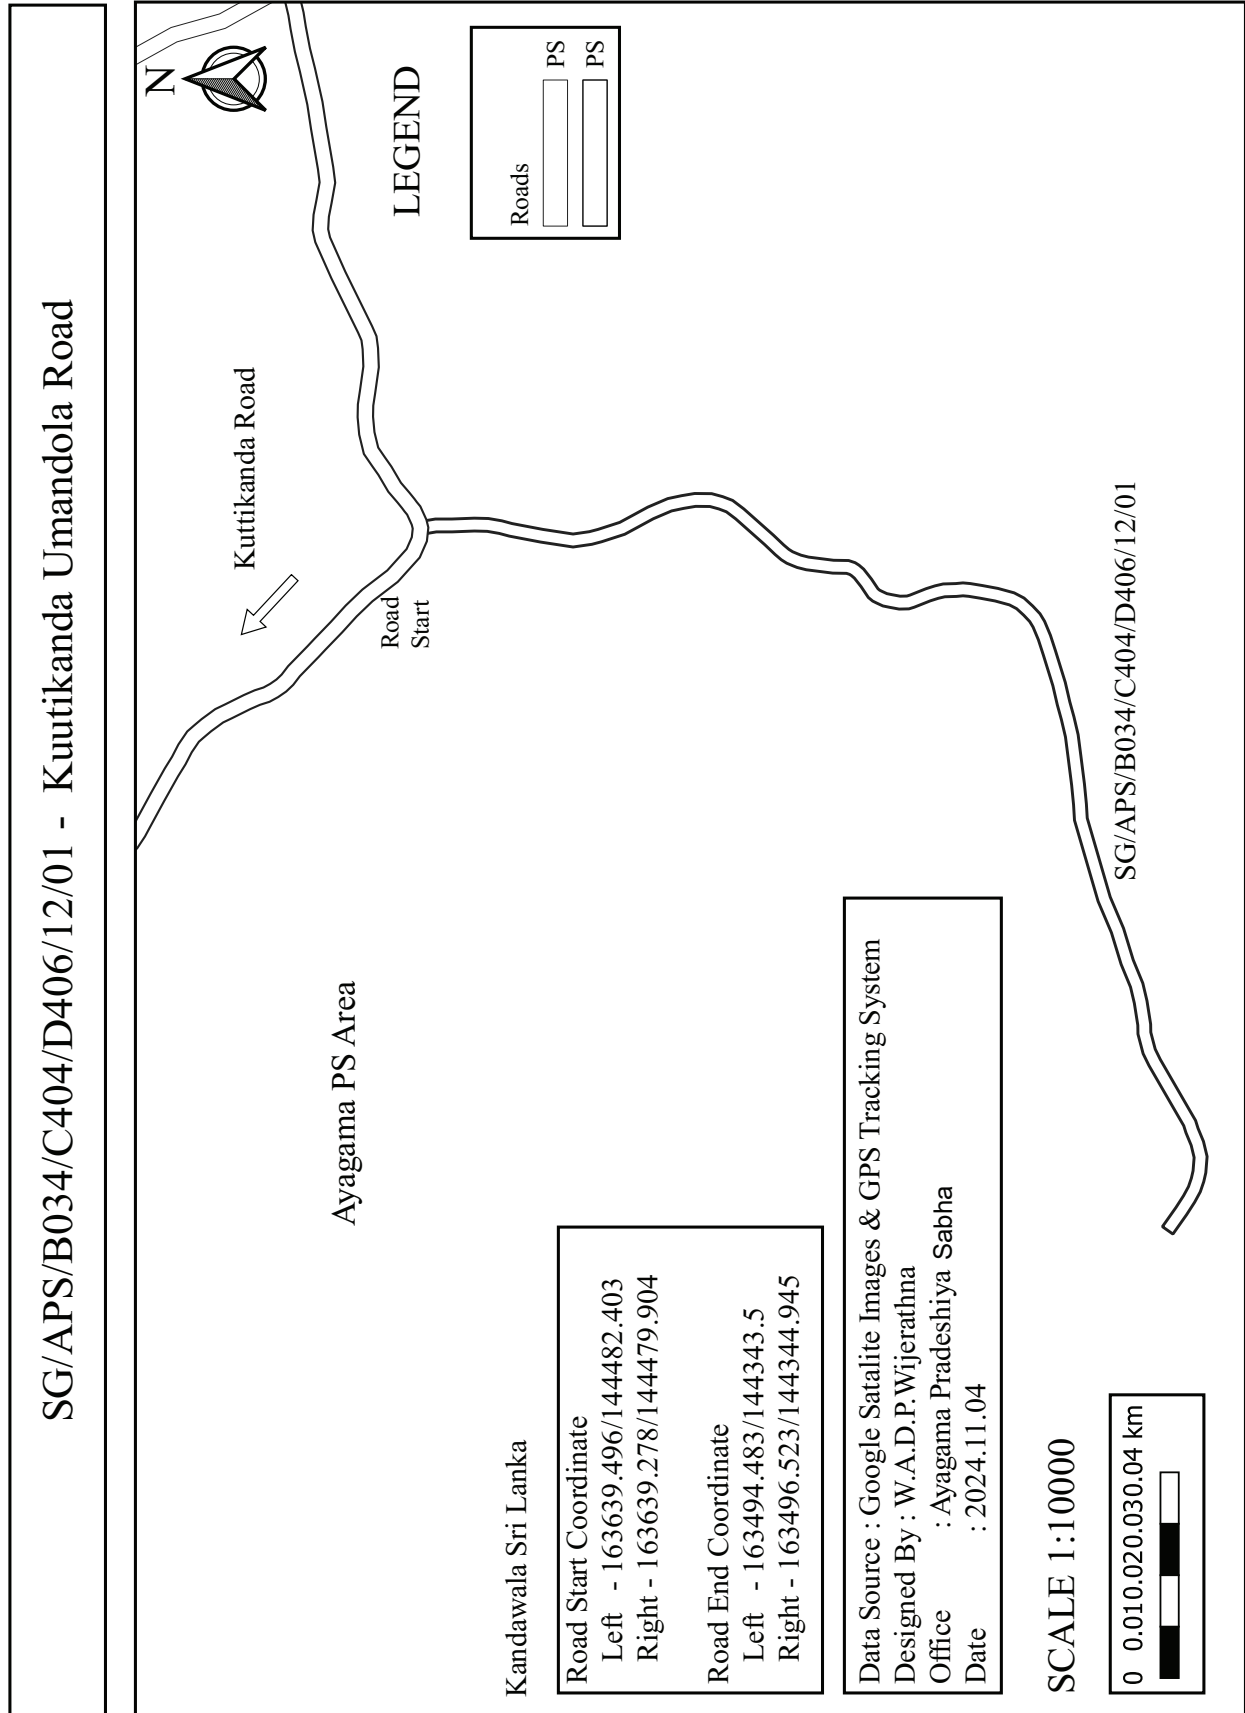


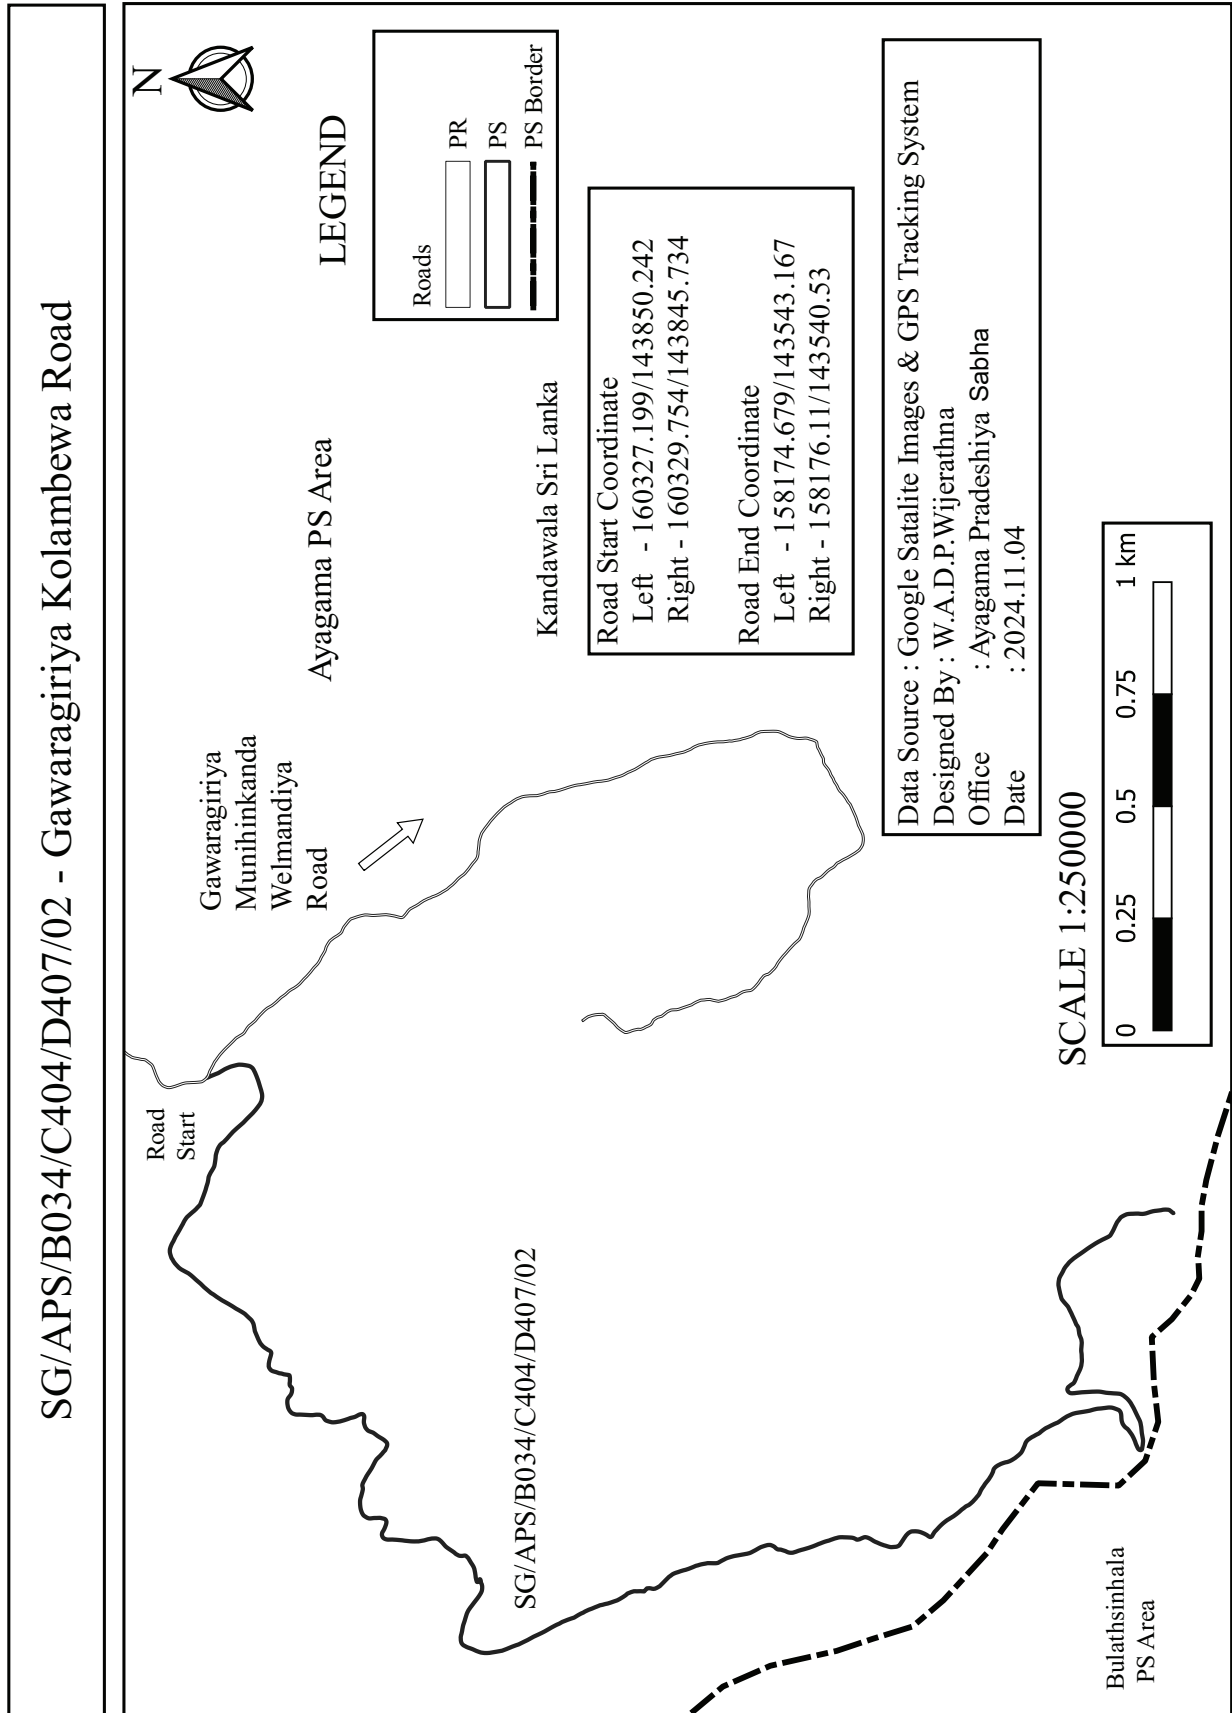





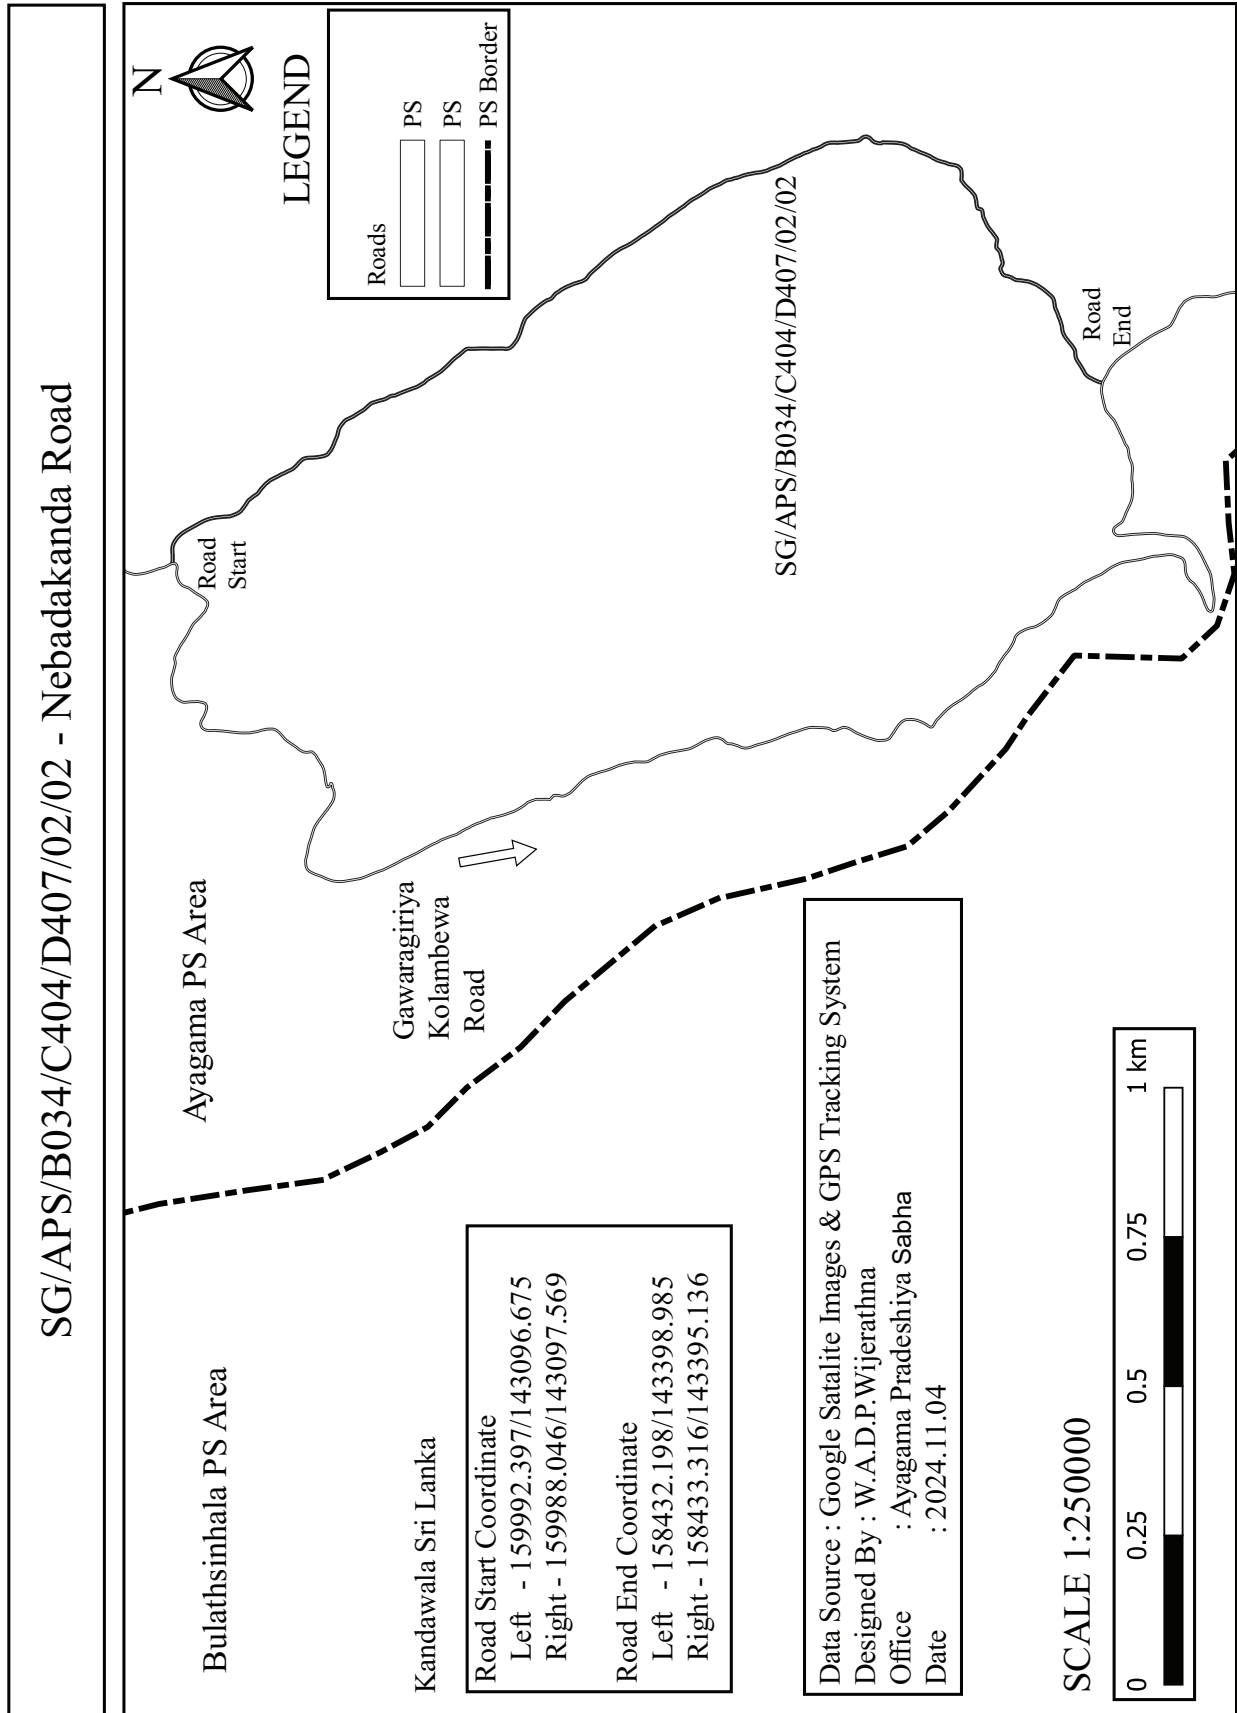


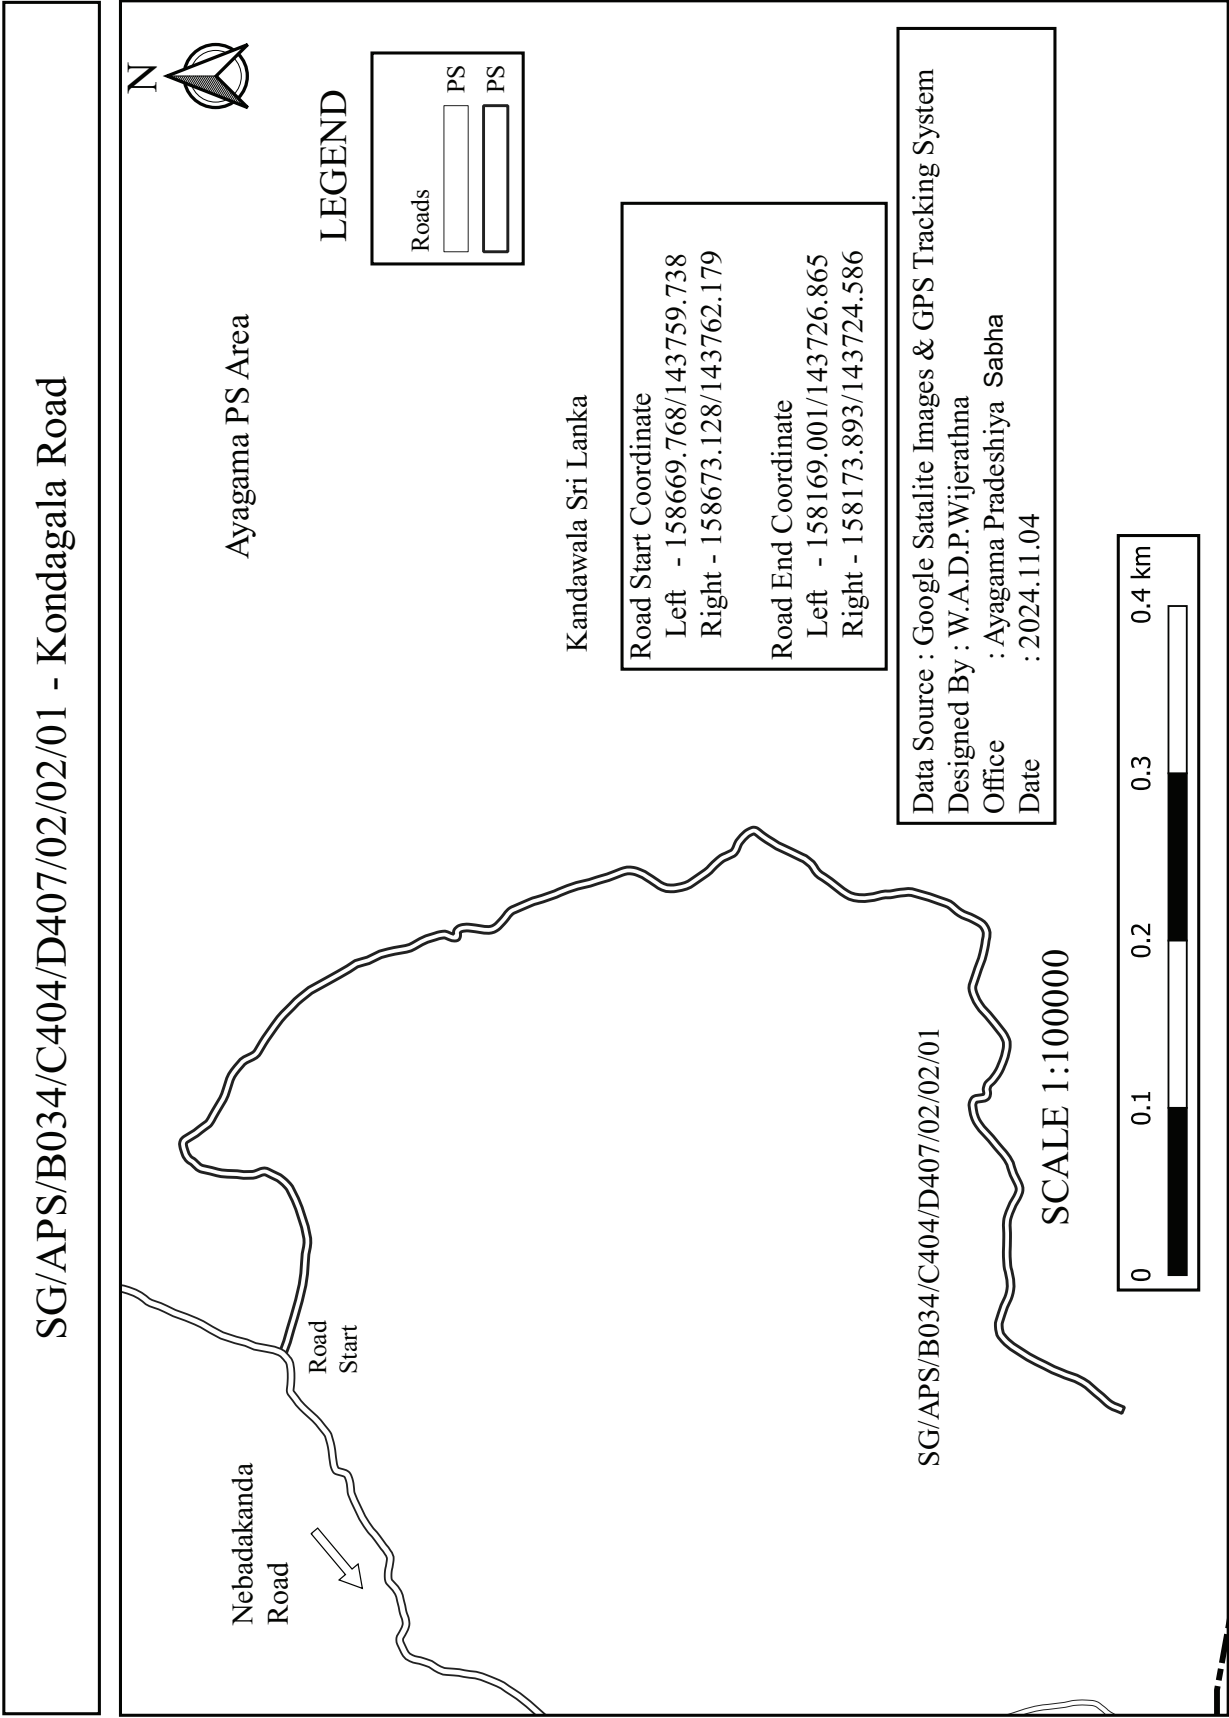


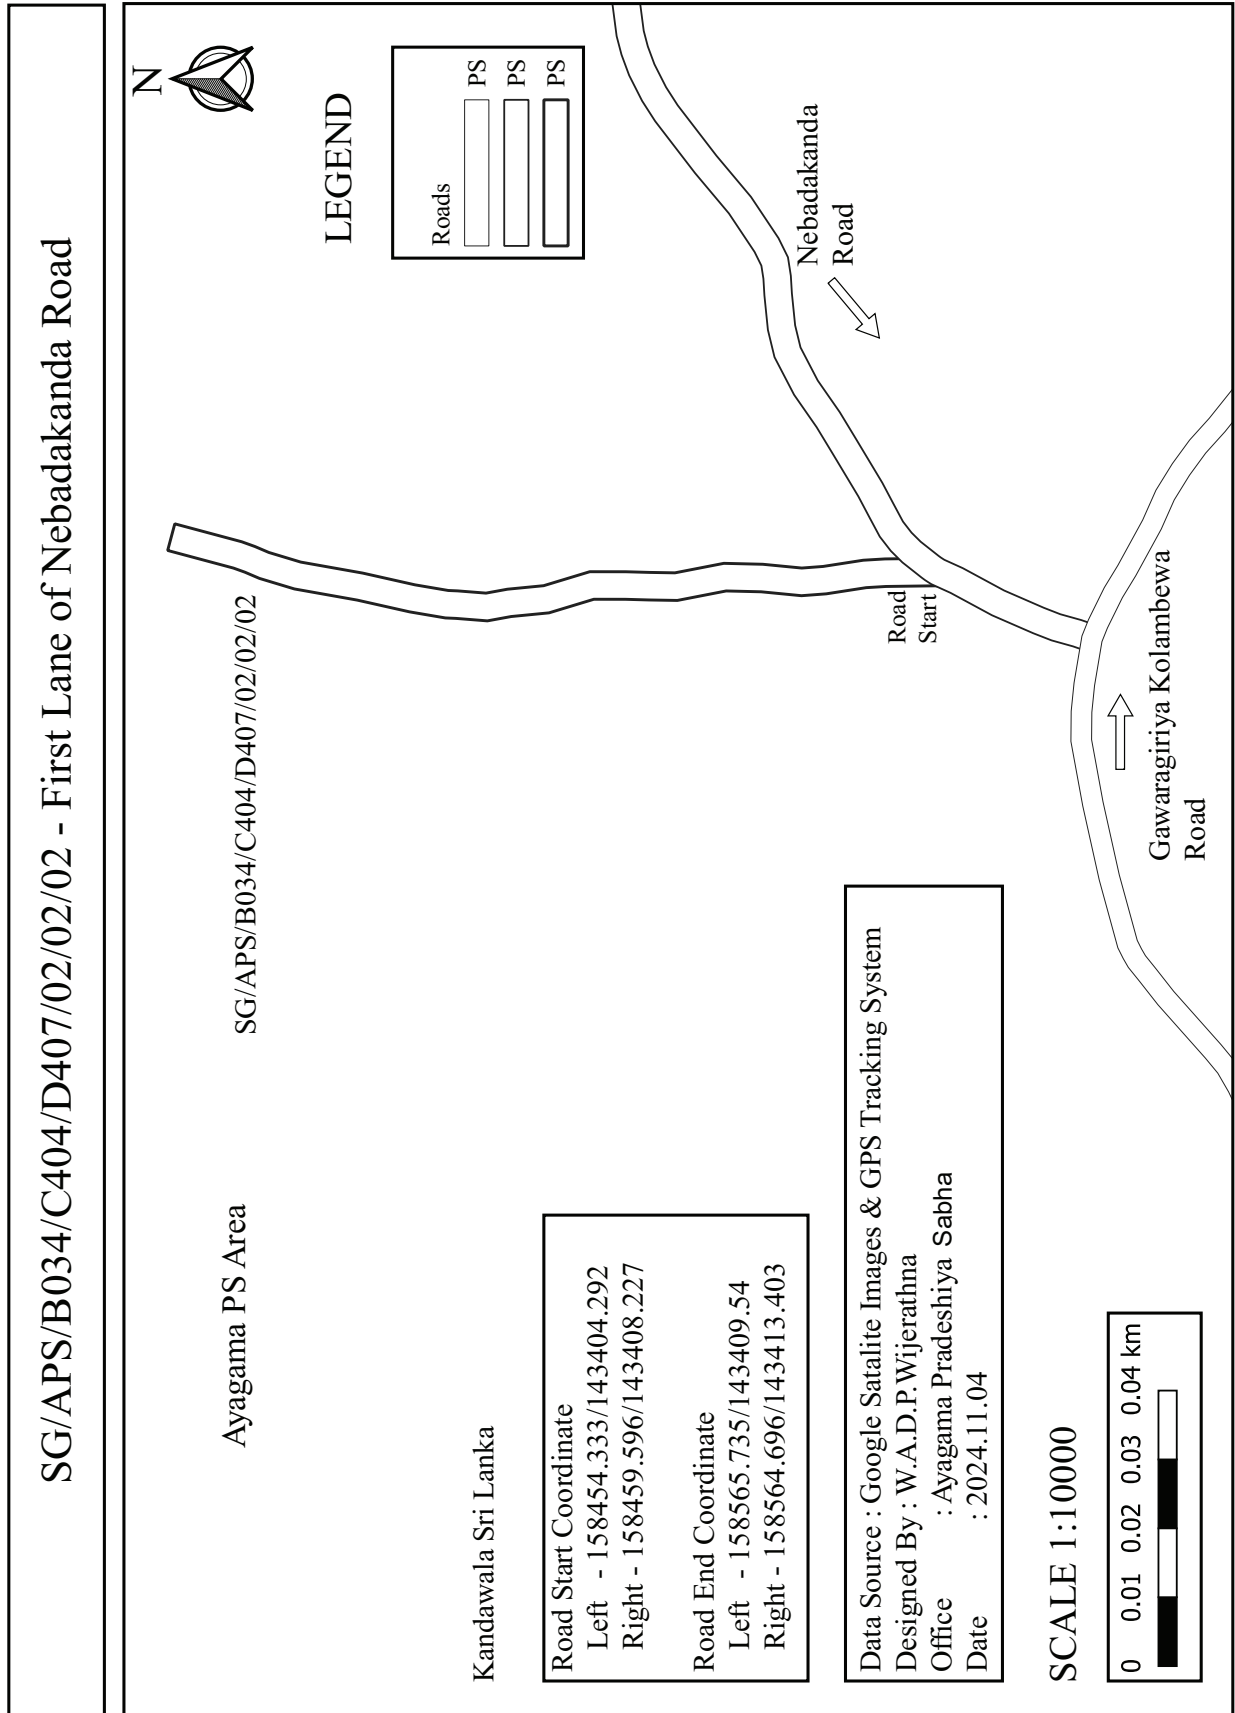

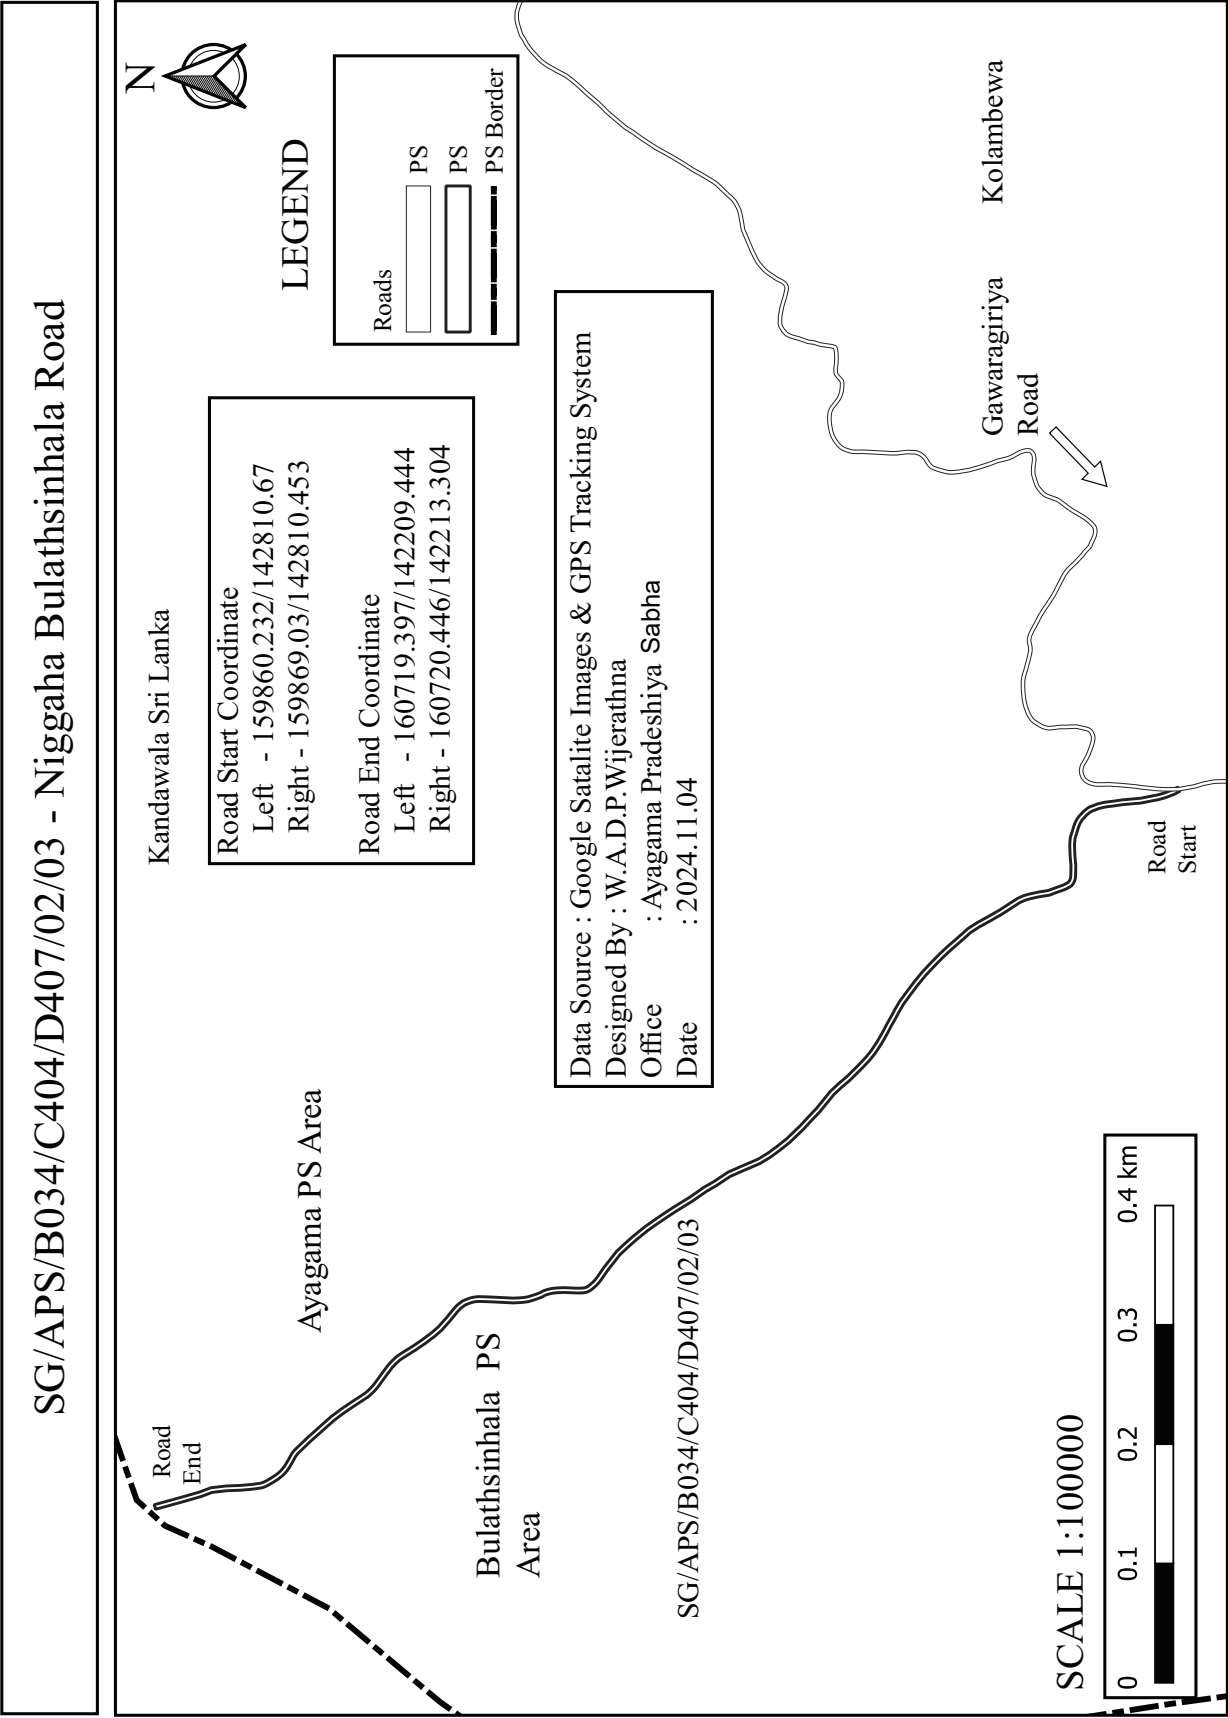


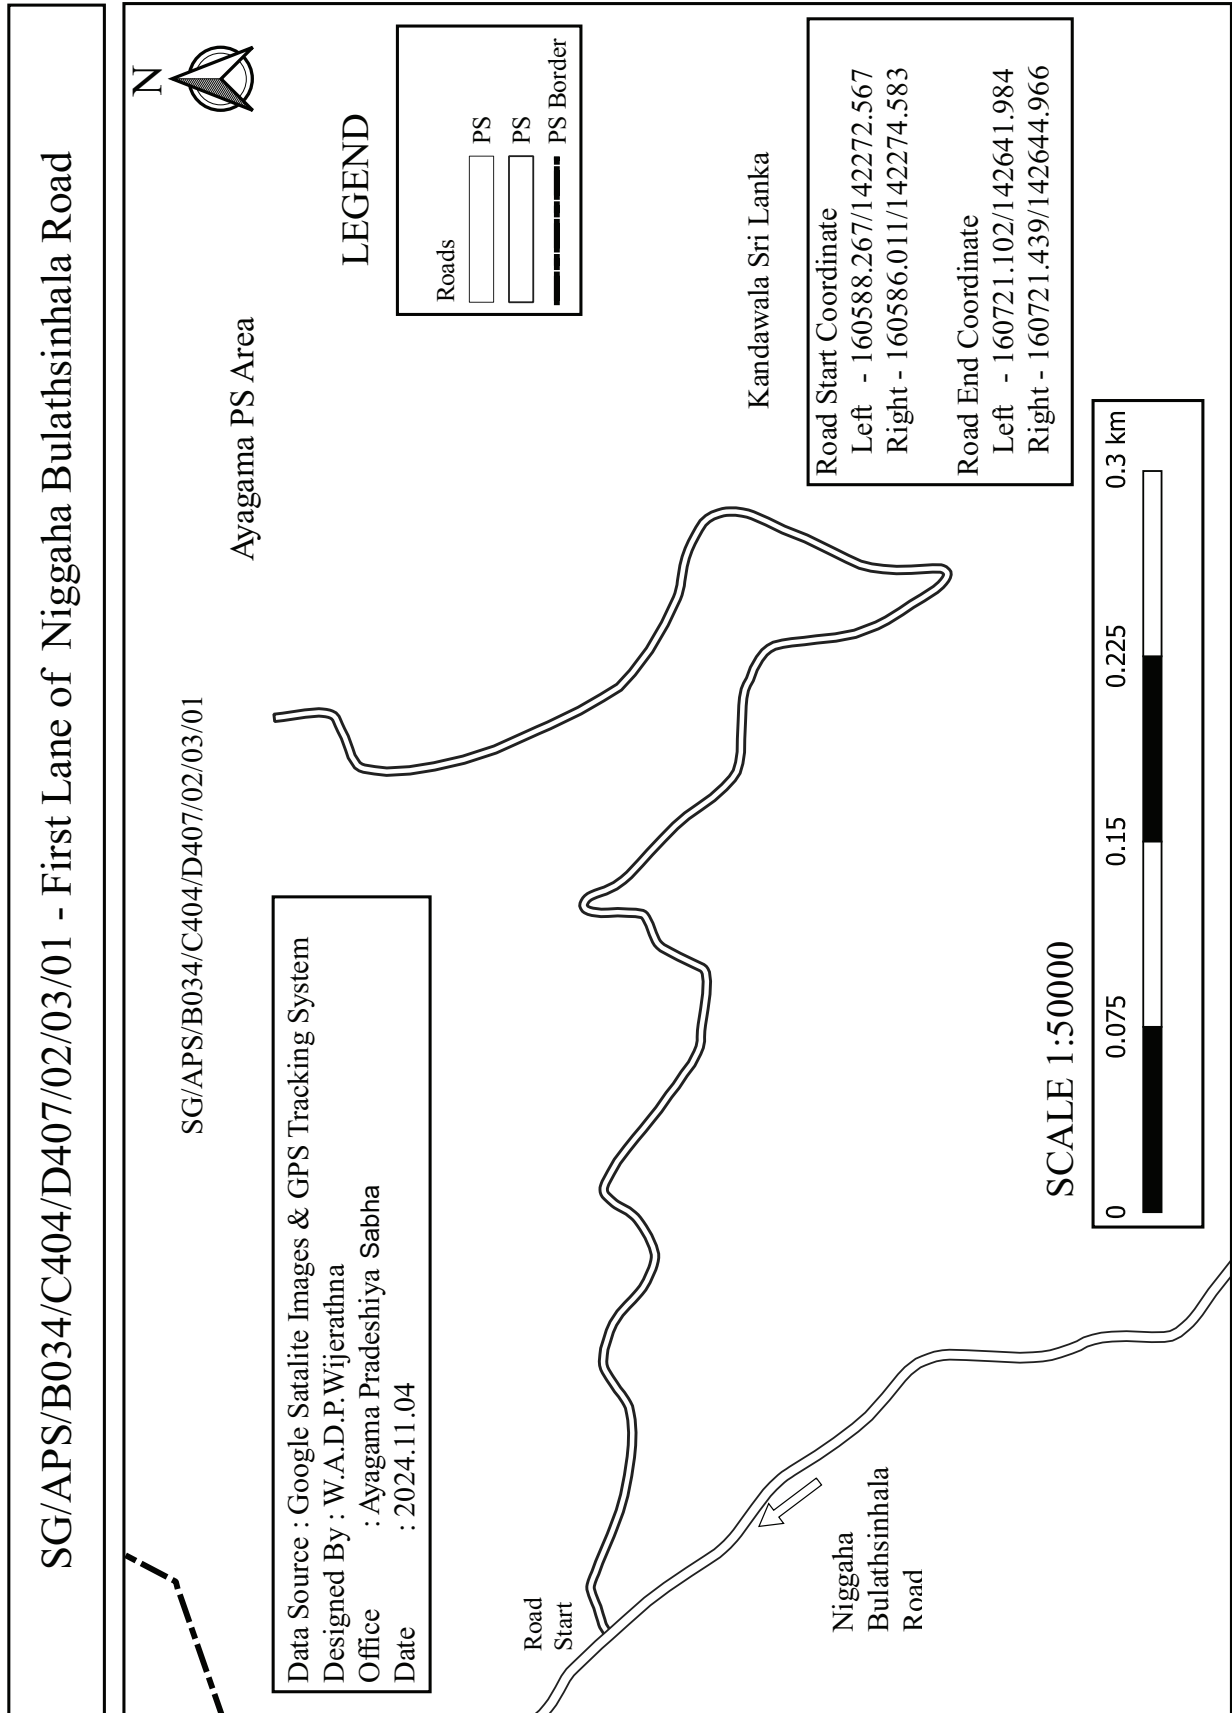


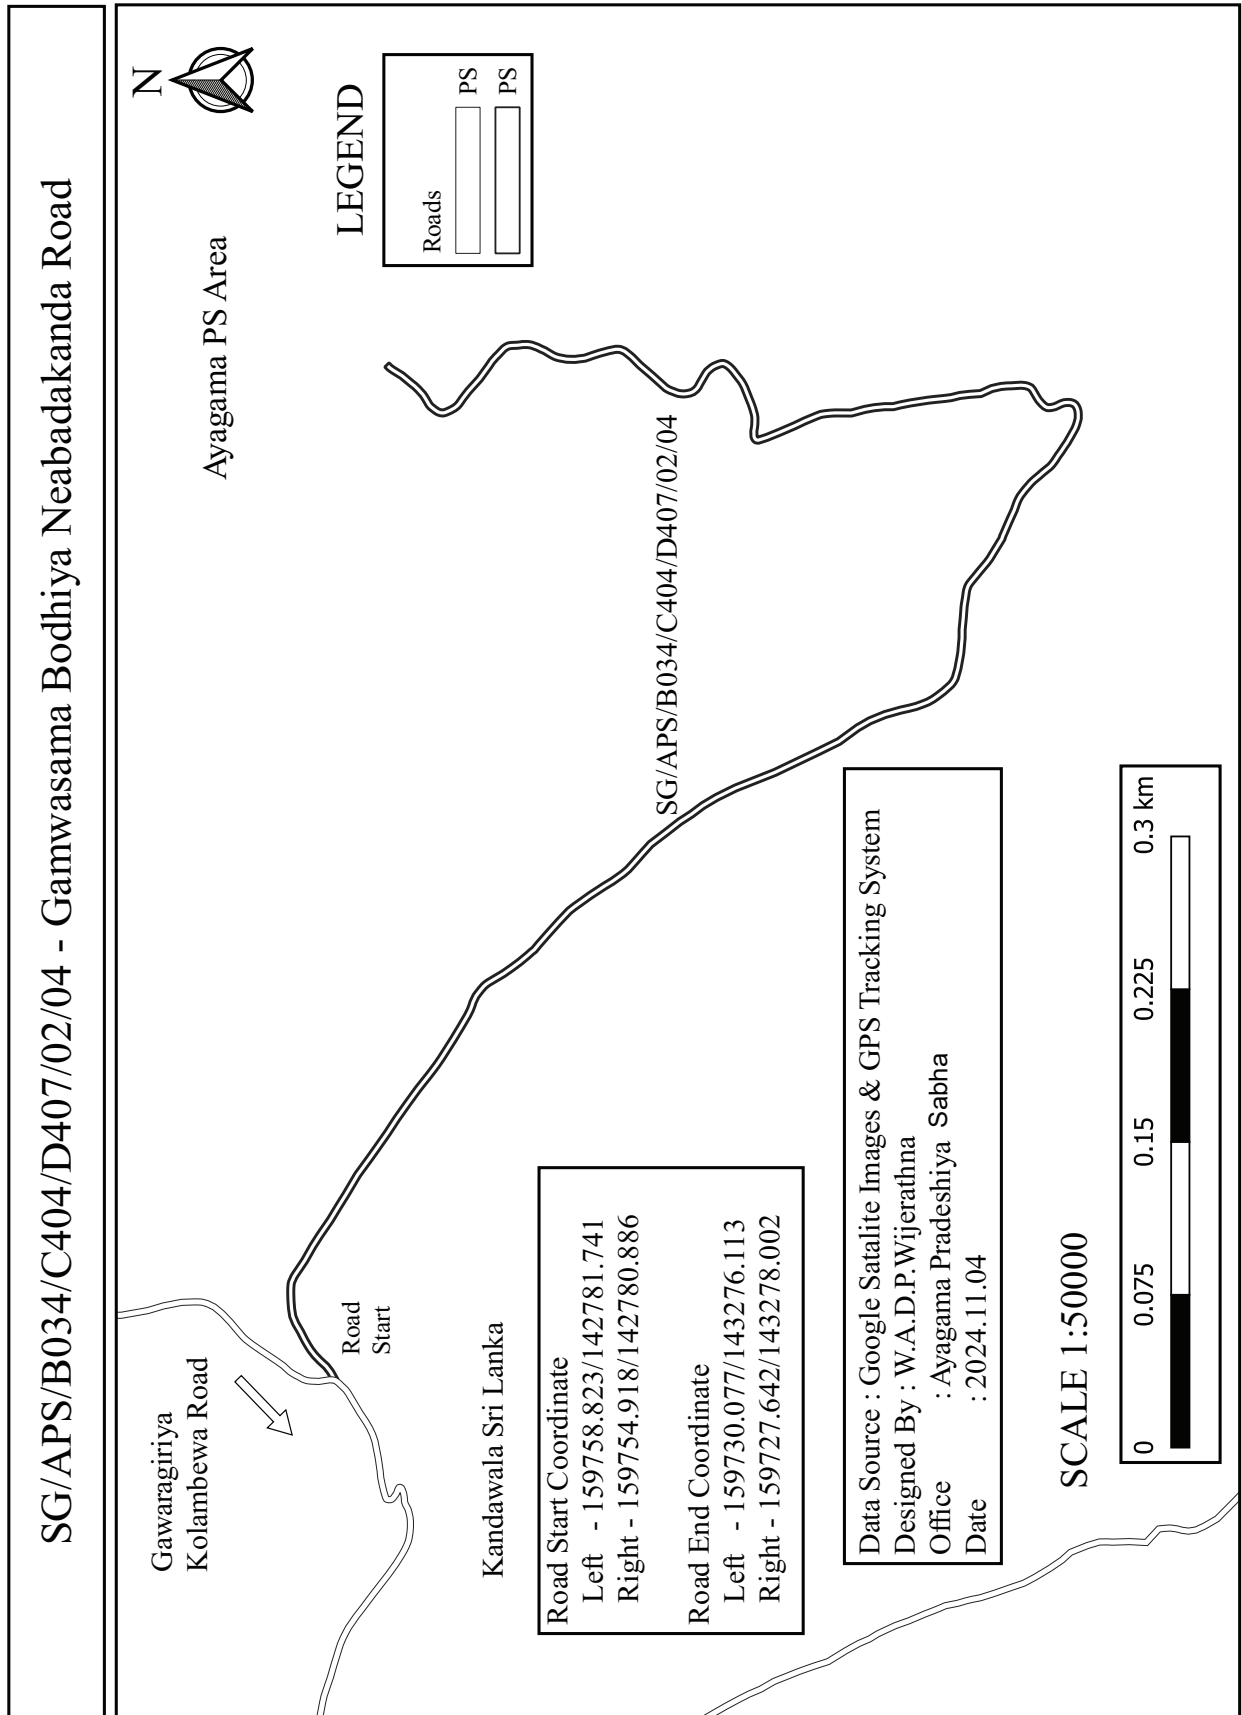

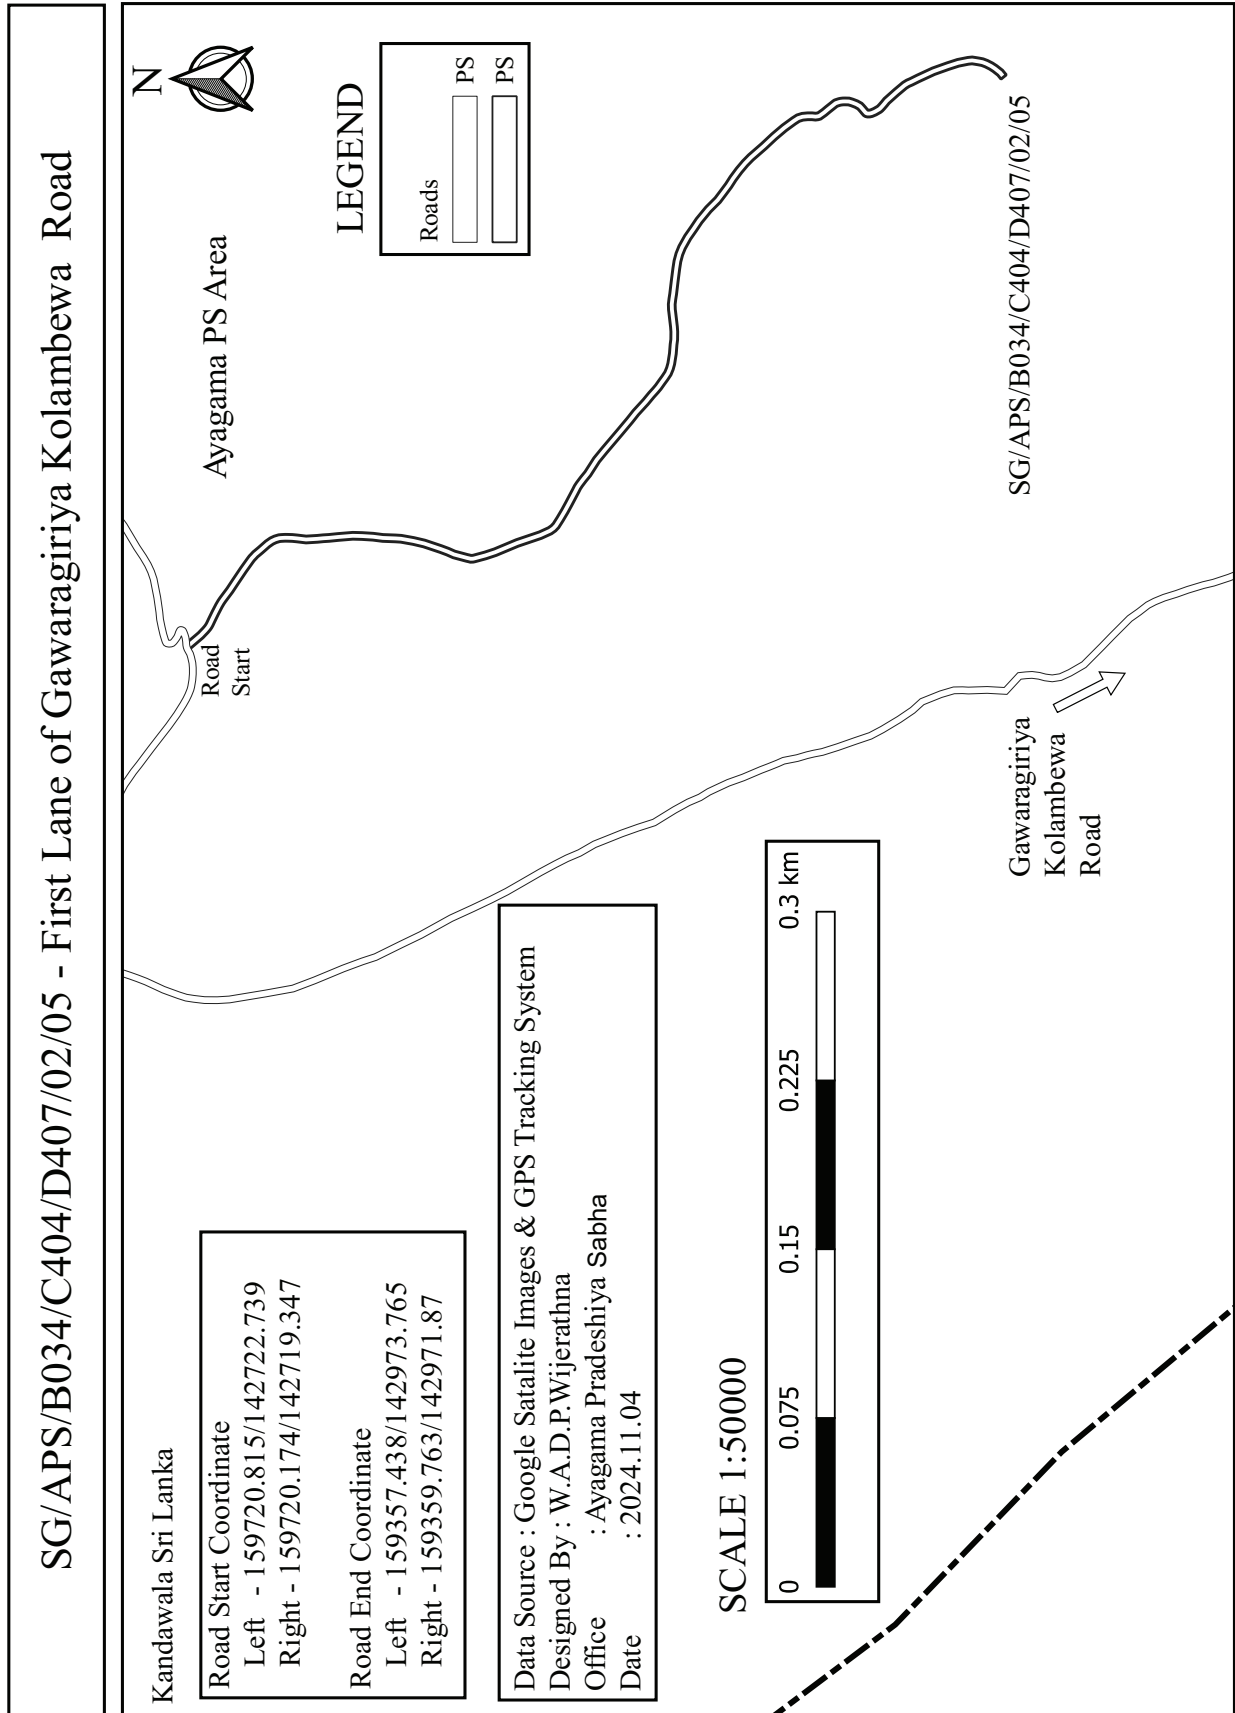




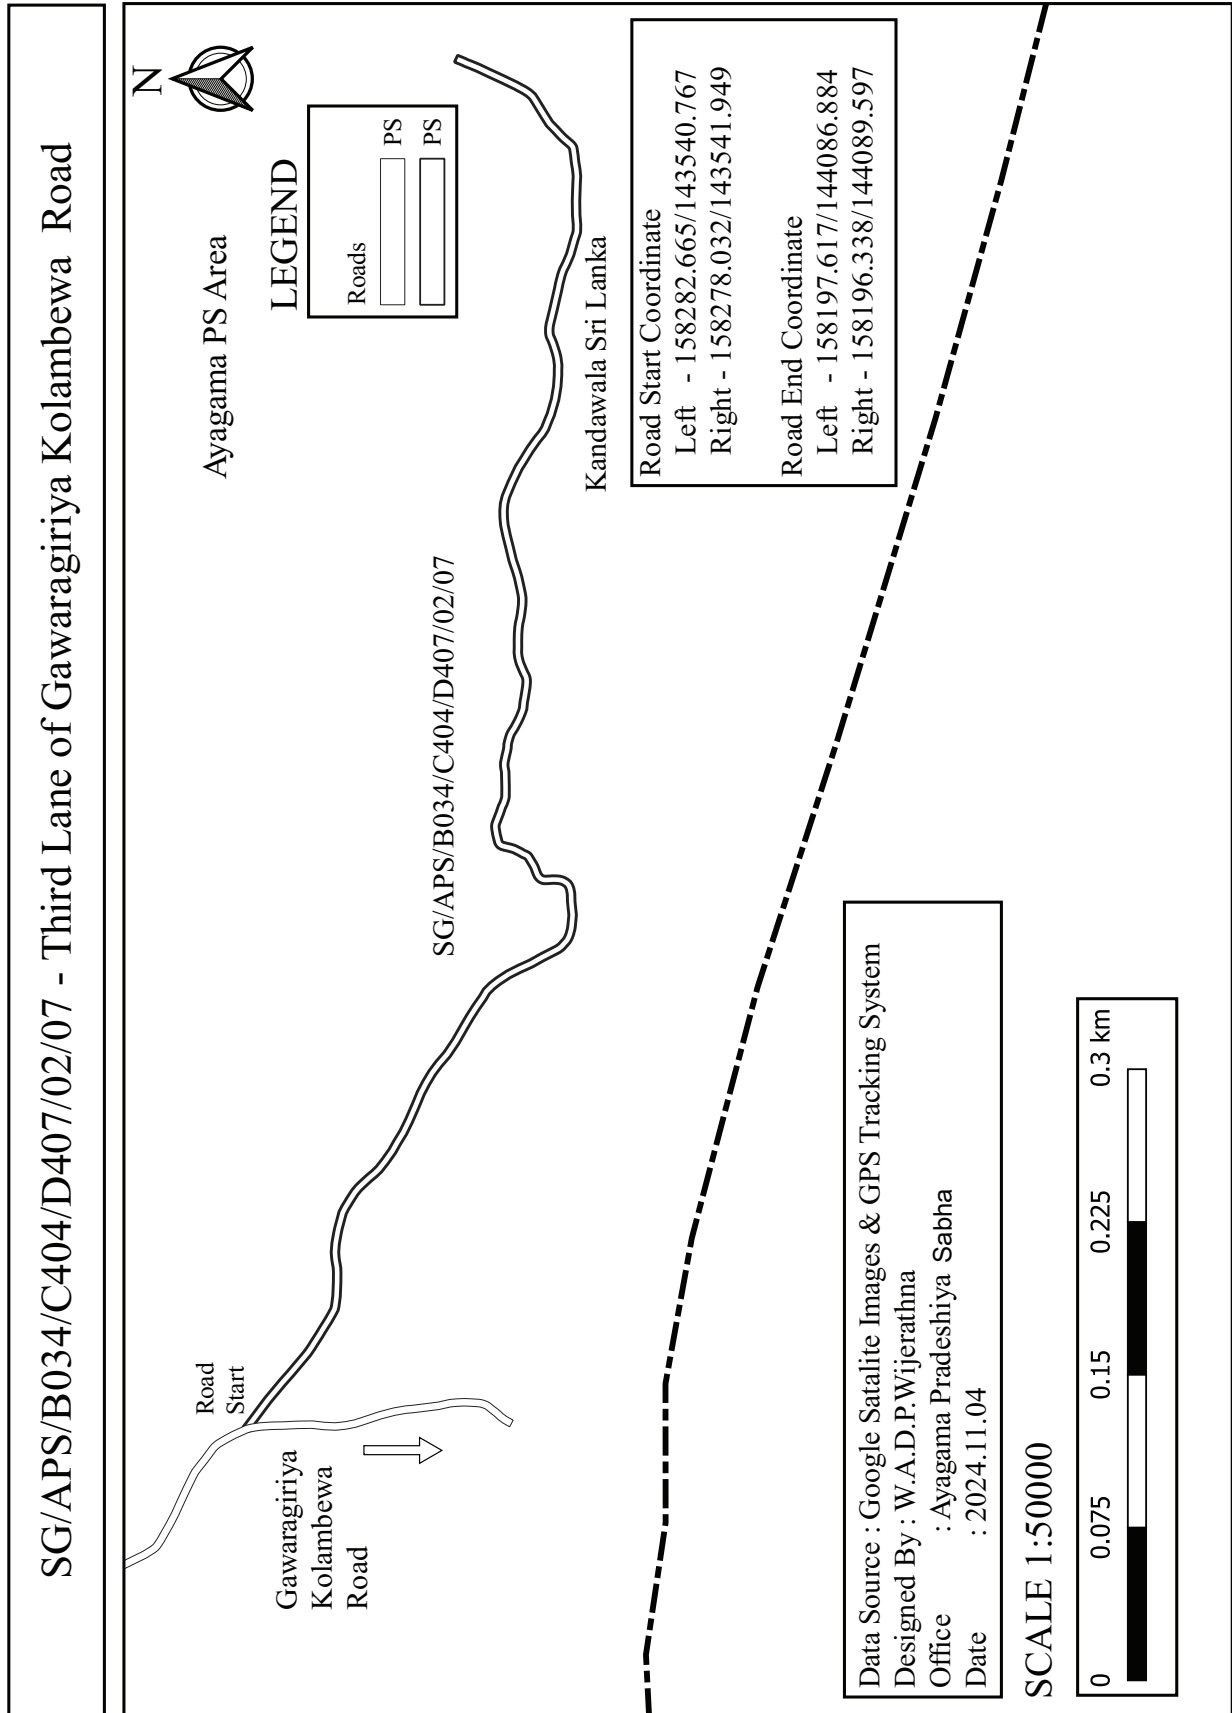


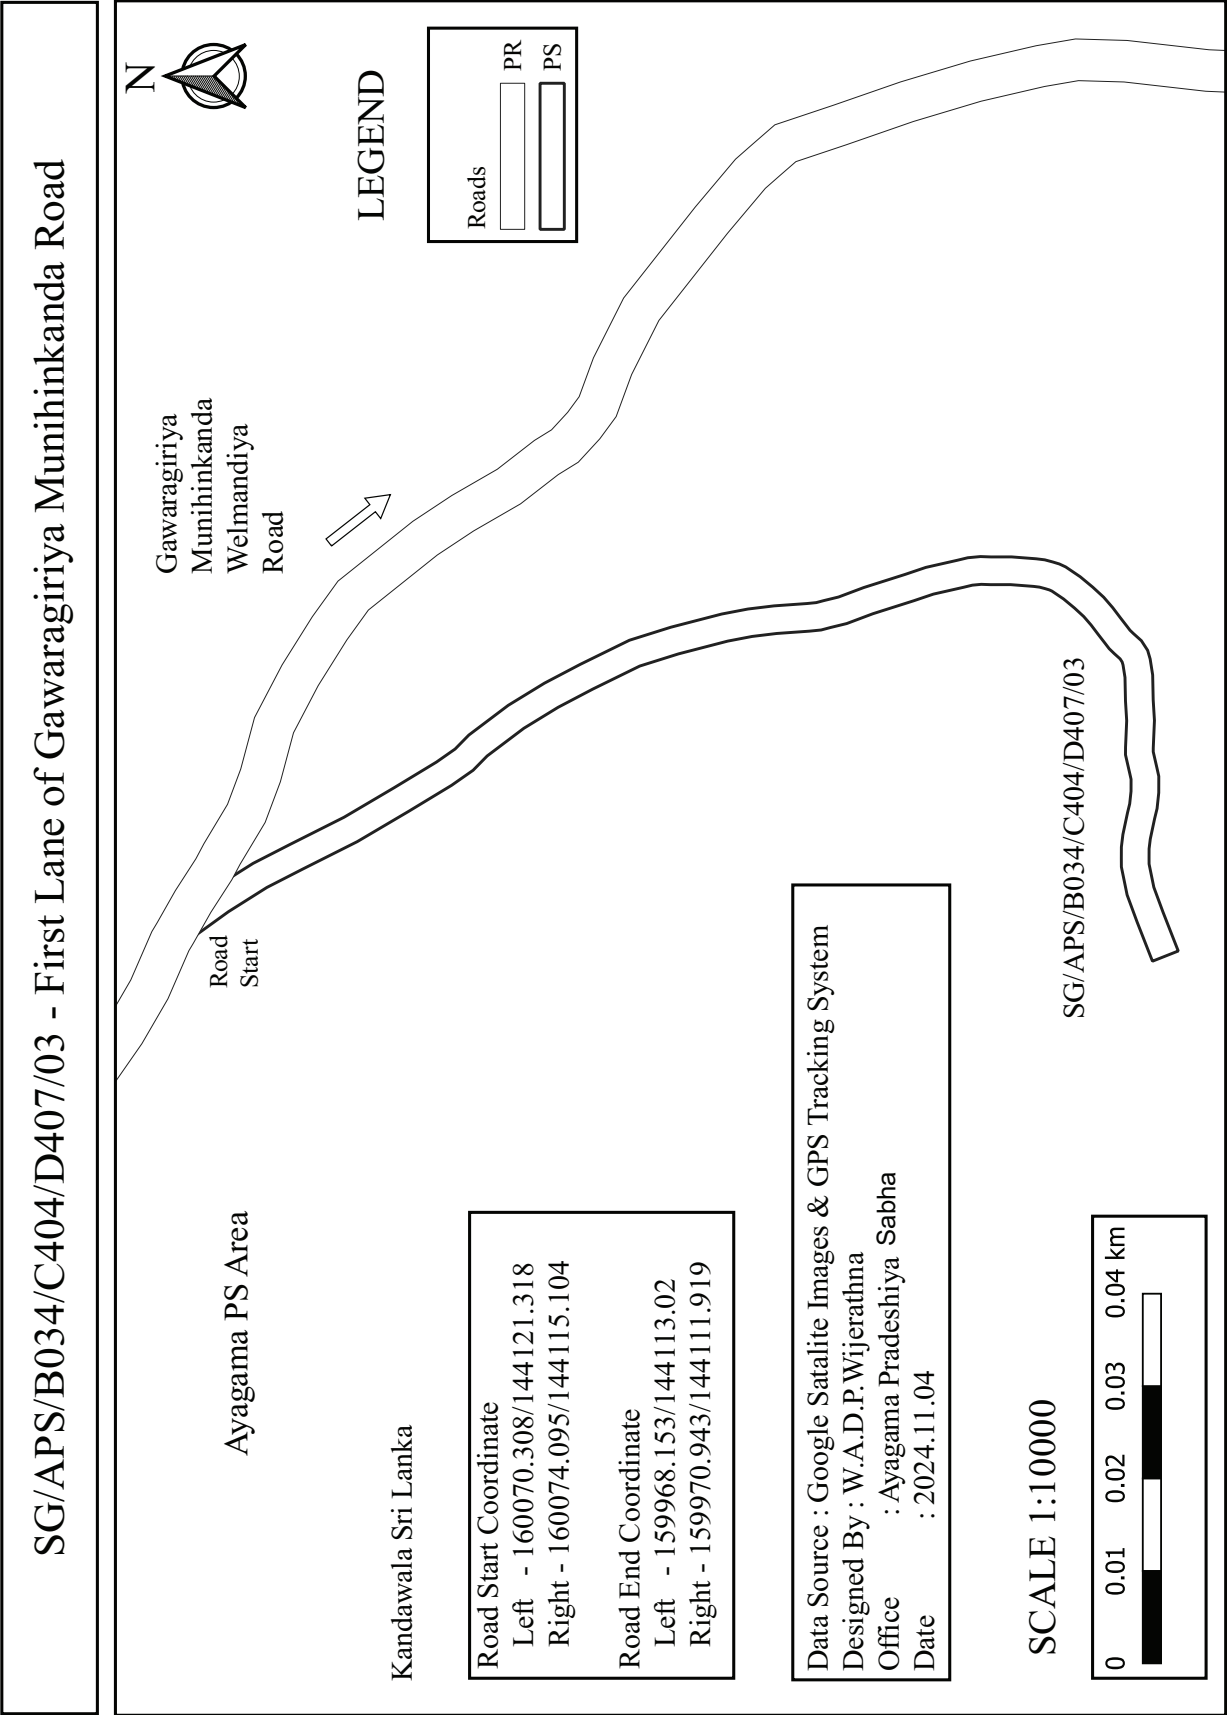


SG/APS/B034/C404/D407/04 - Second Lane of Kolambewa Munihinkanda Road

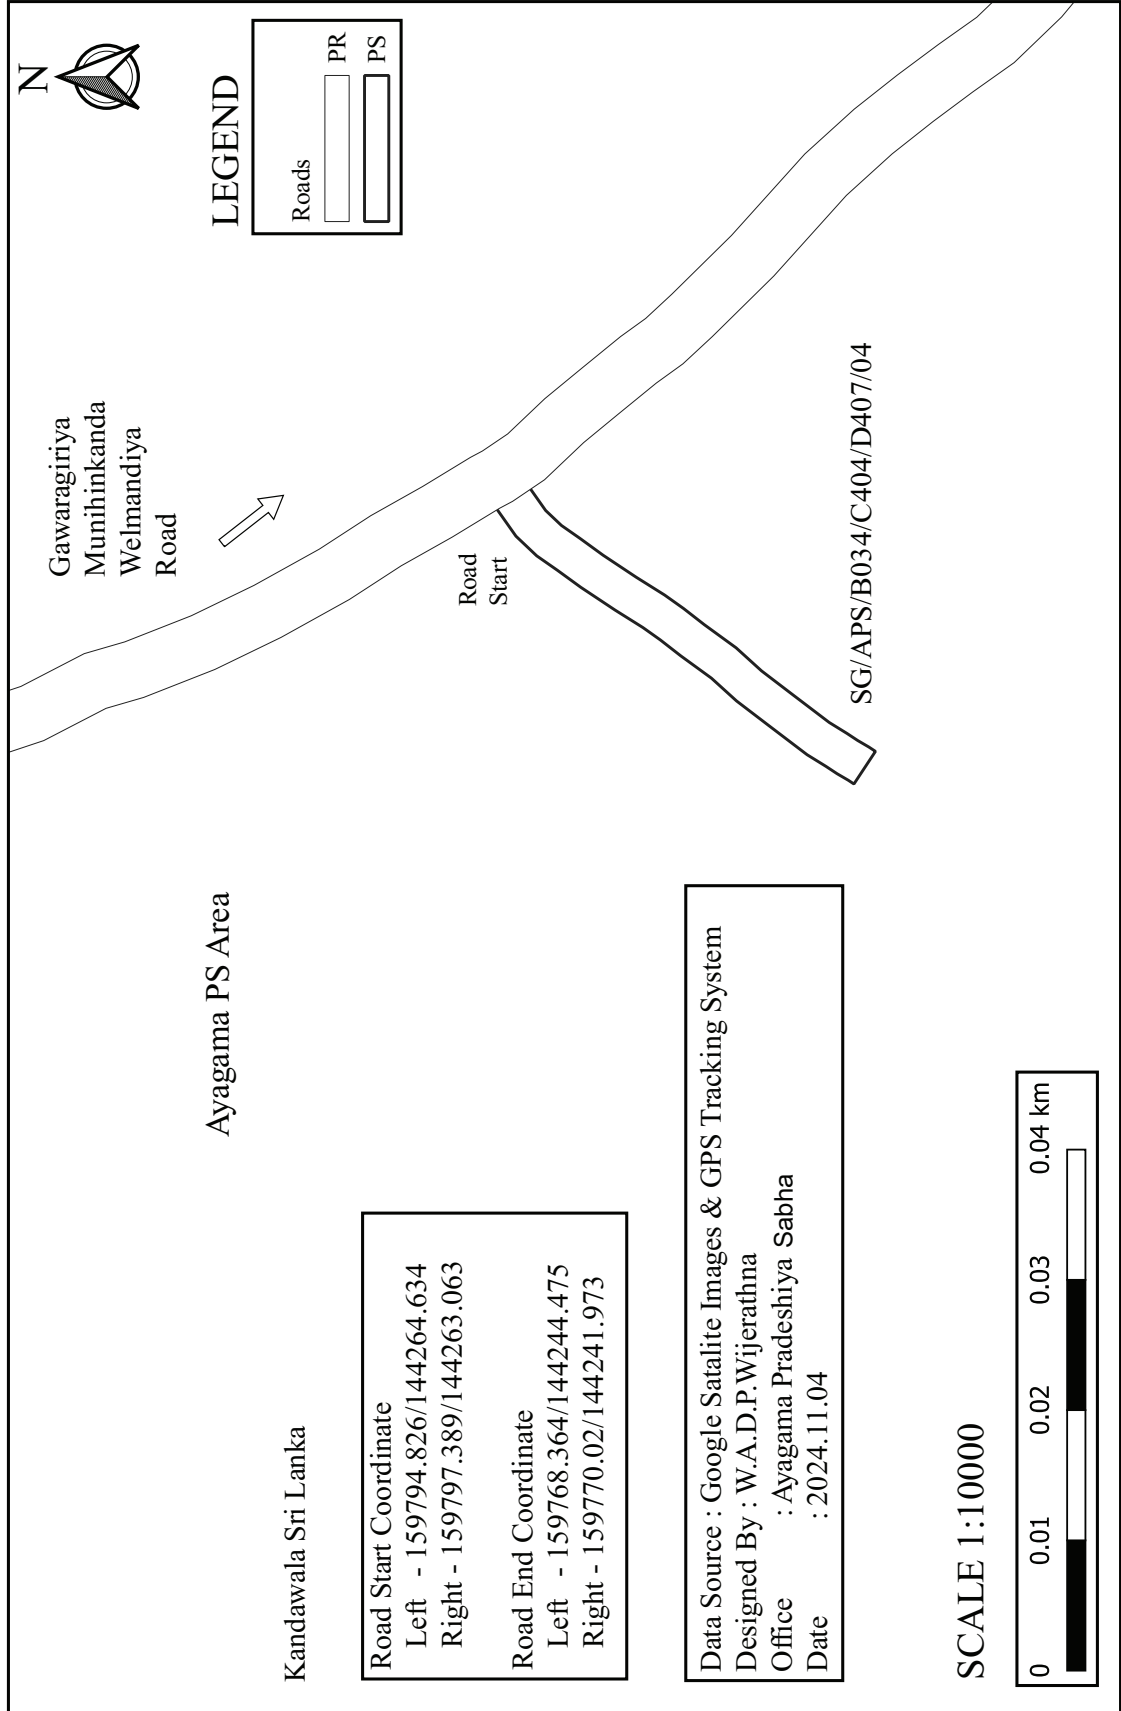



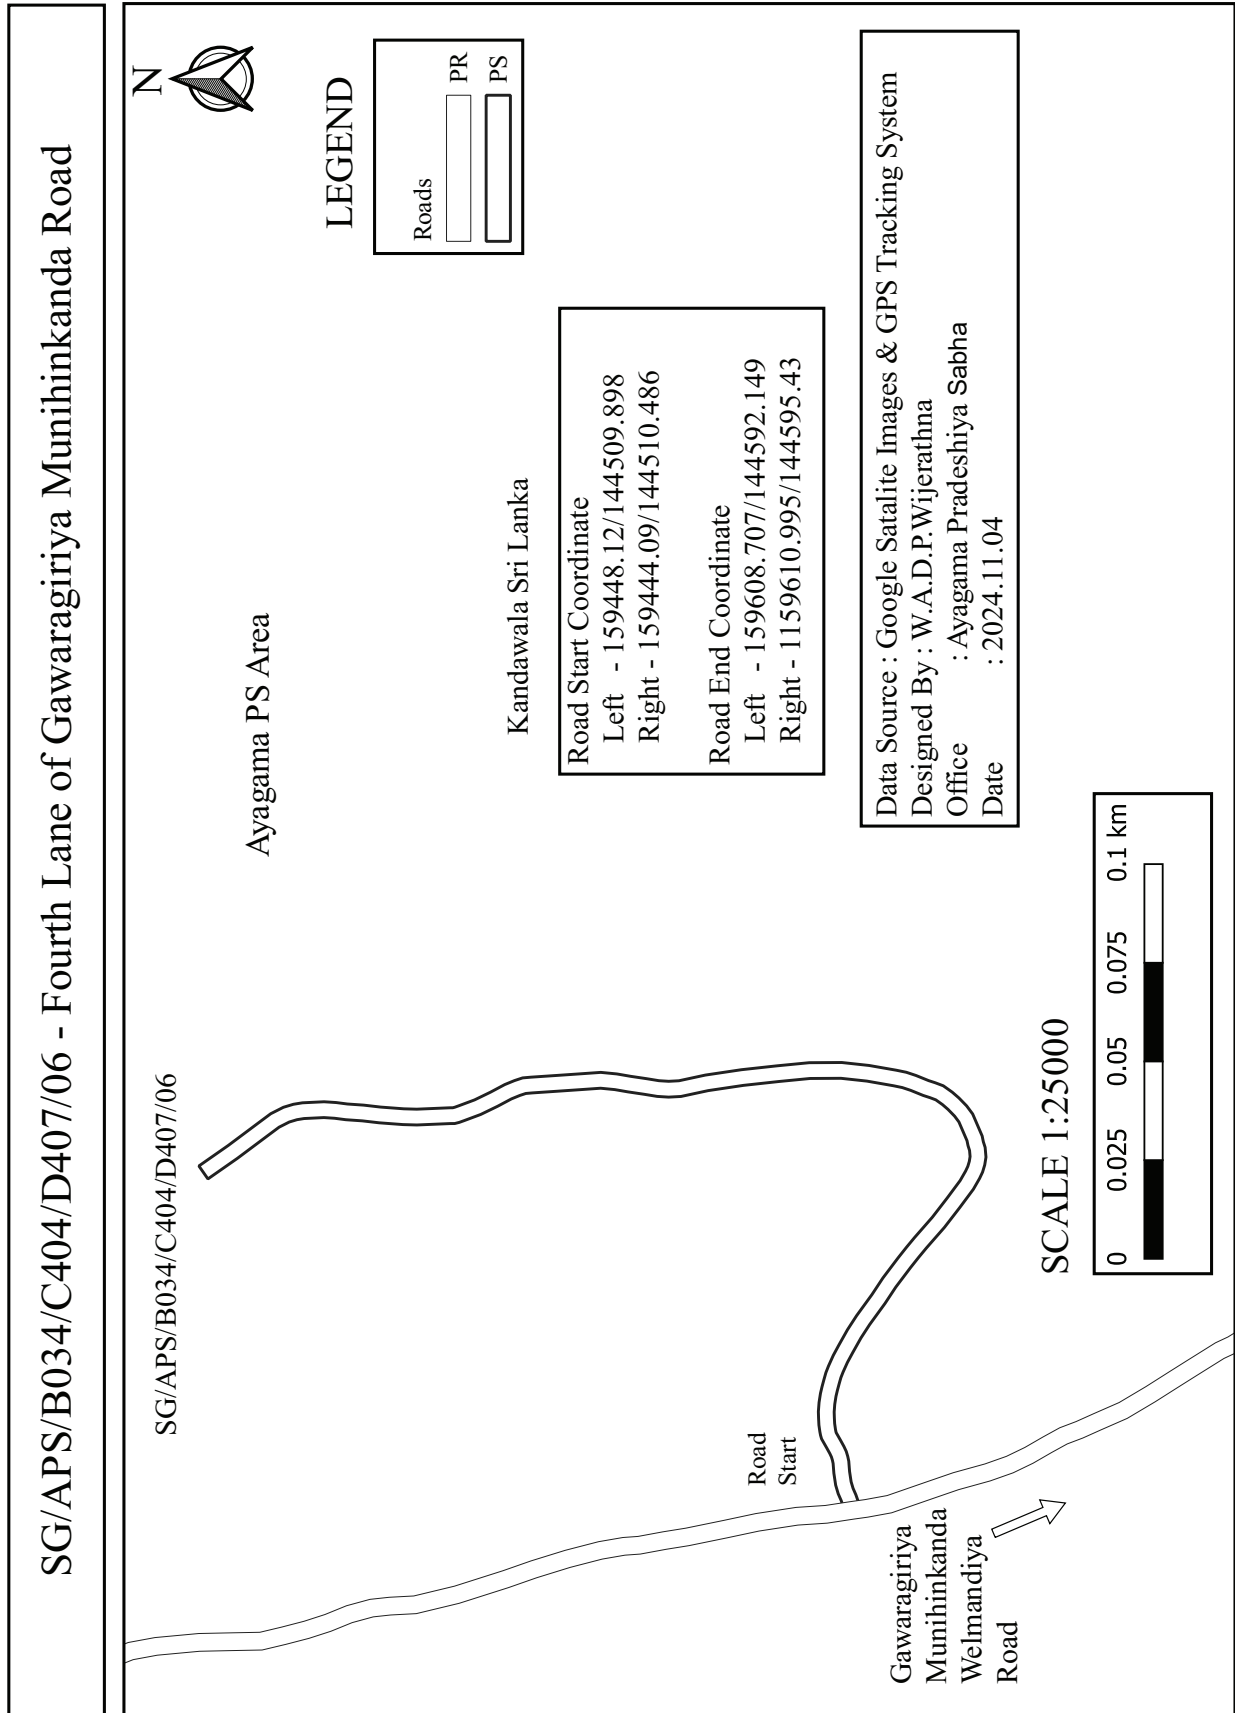





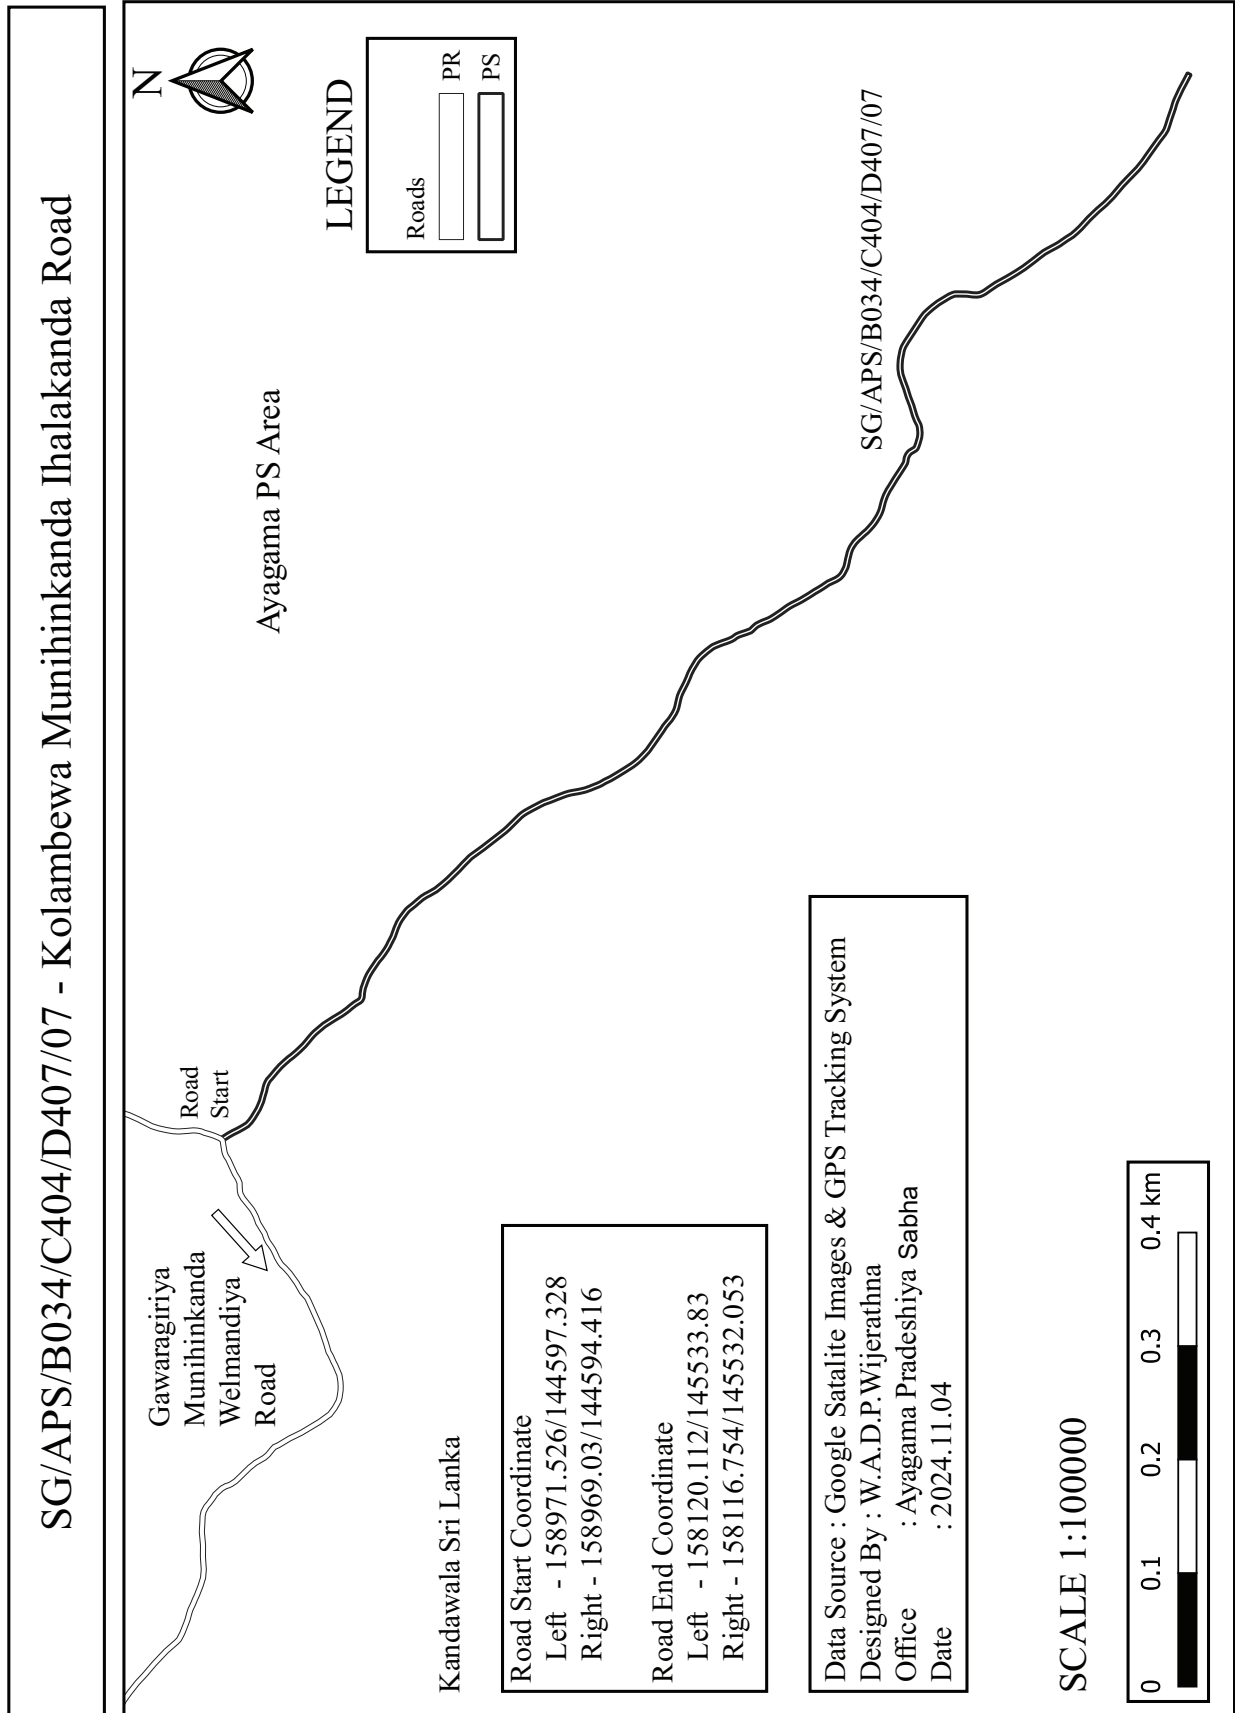






SG/APS/B034/C404/D407/07/02 - Kolambewa Munihinkanda Dodamgewaththa Road

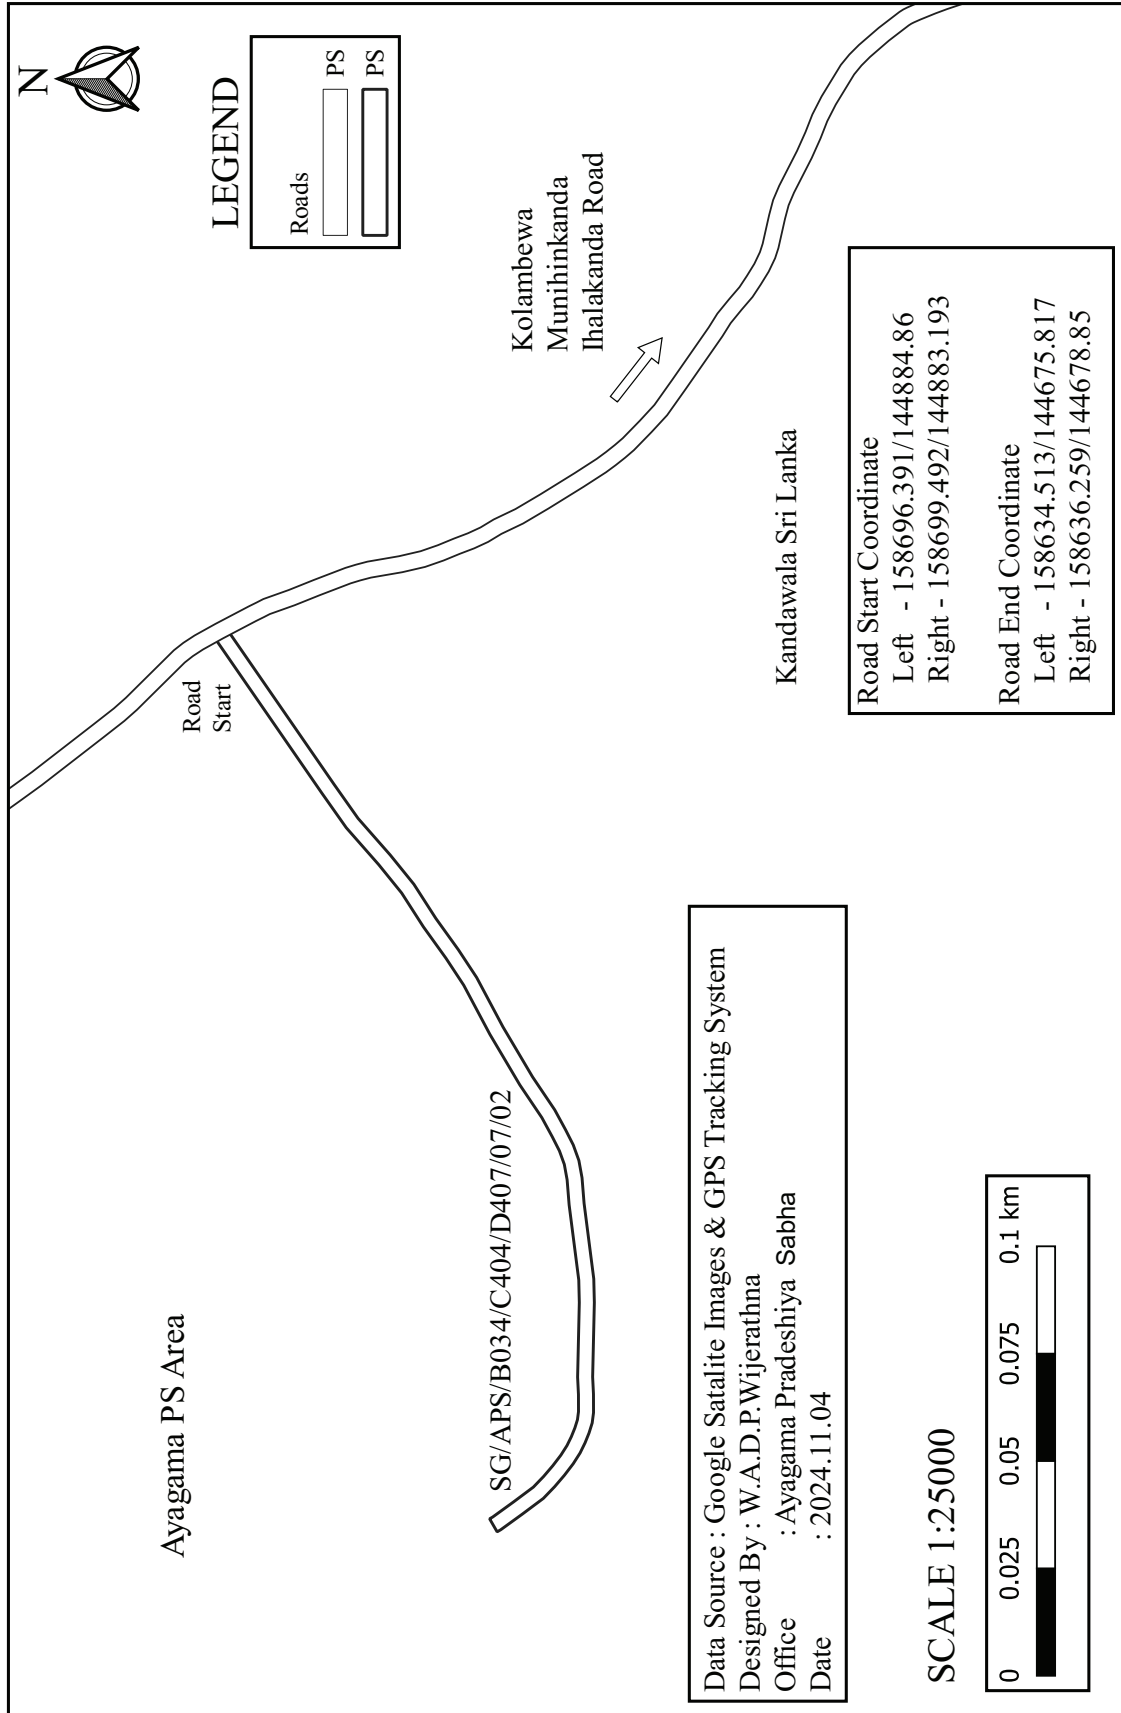


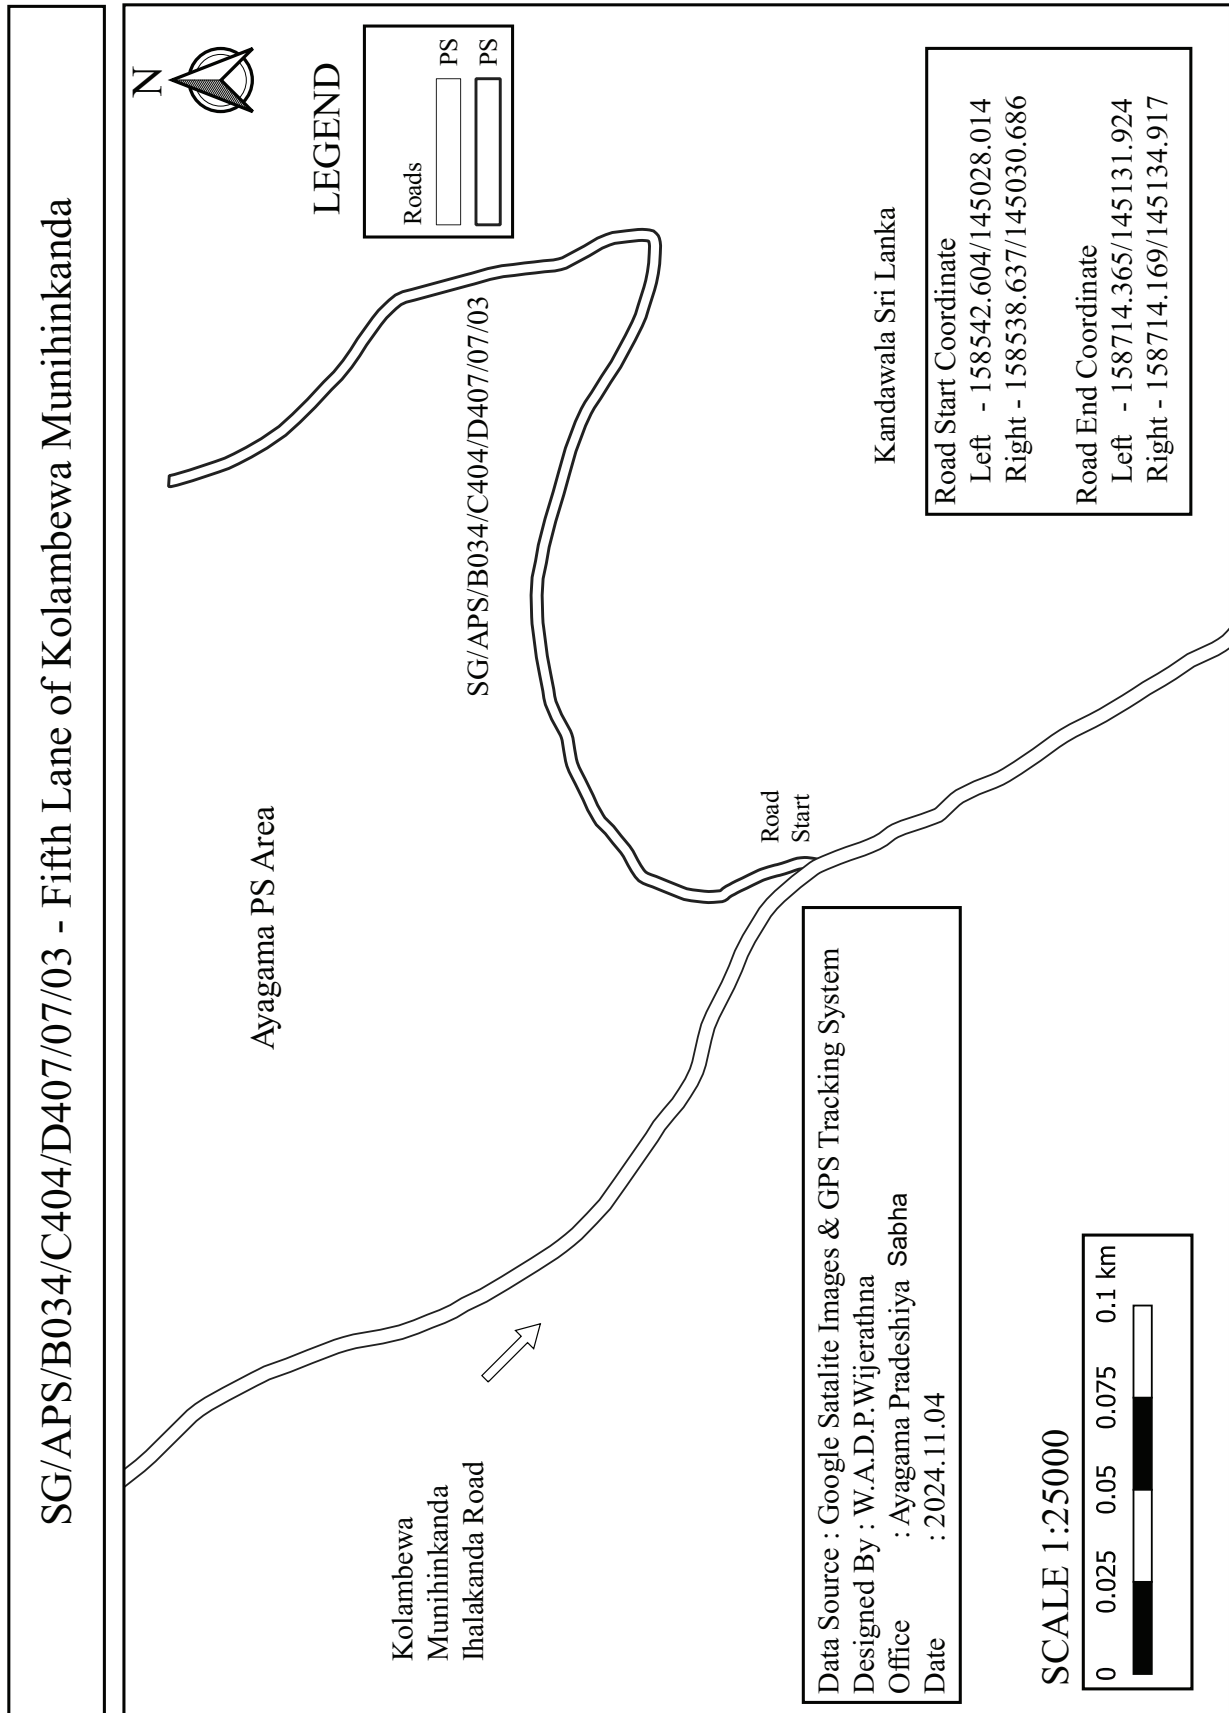


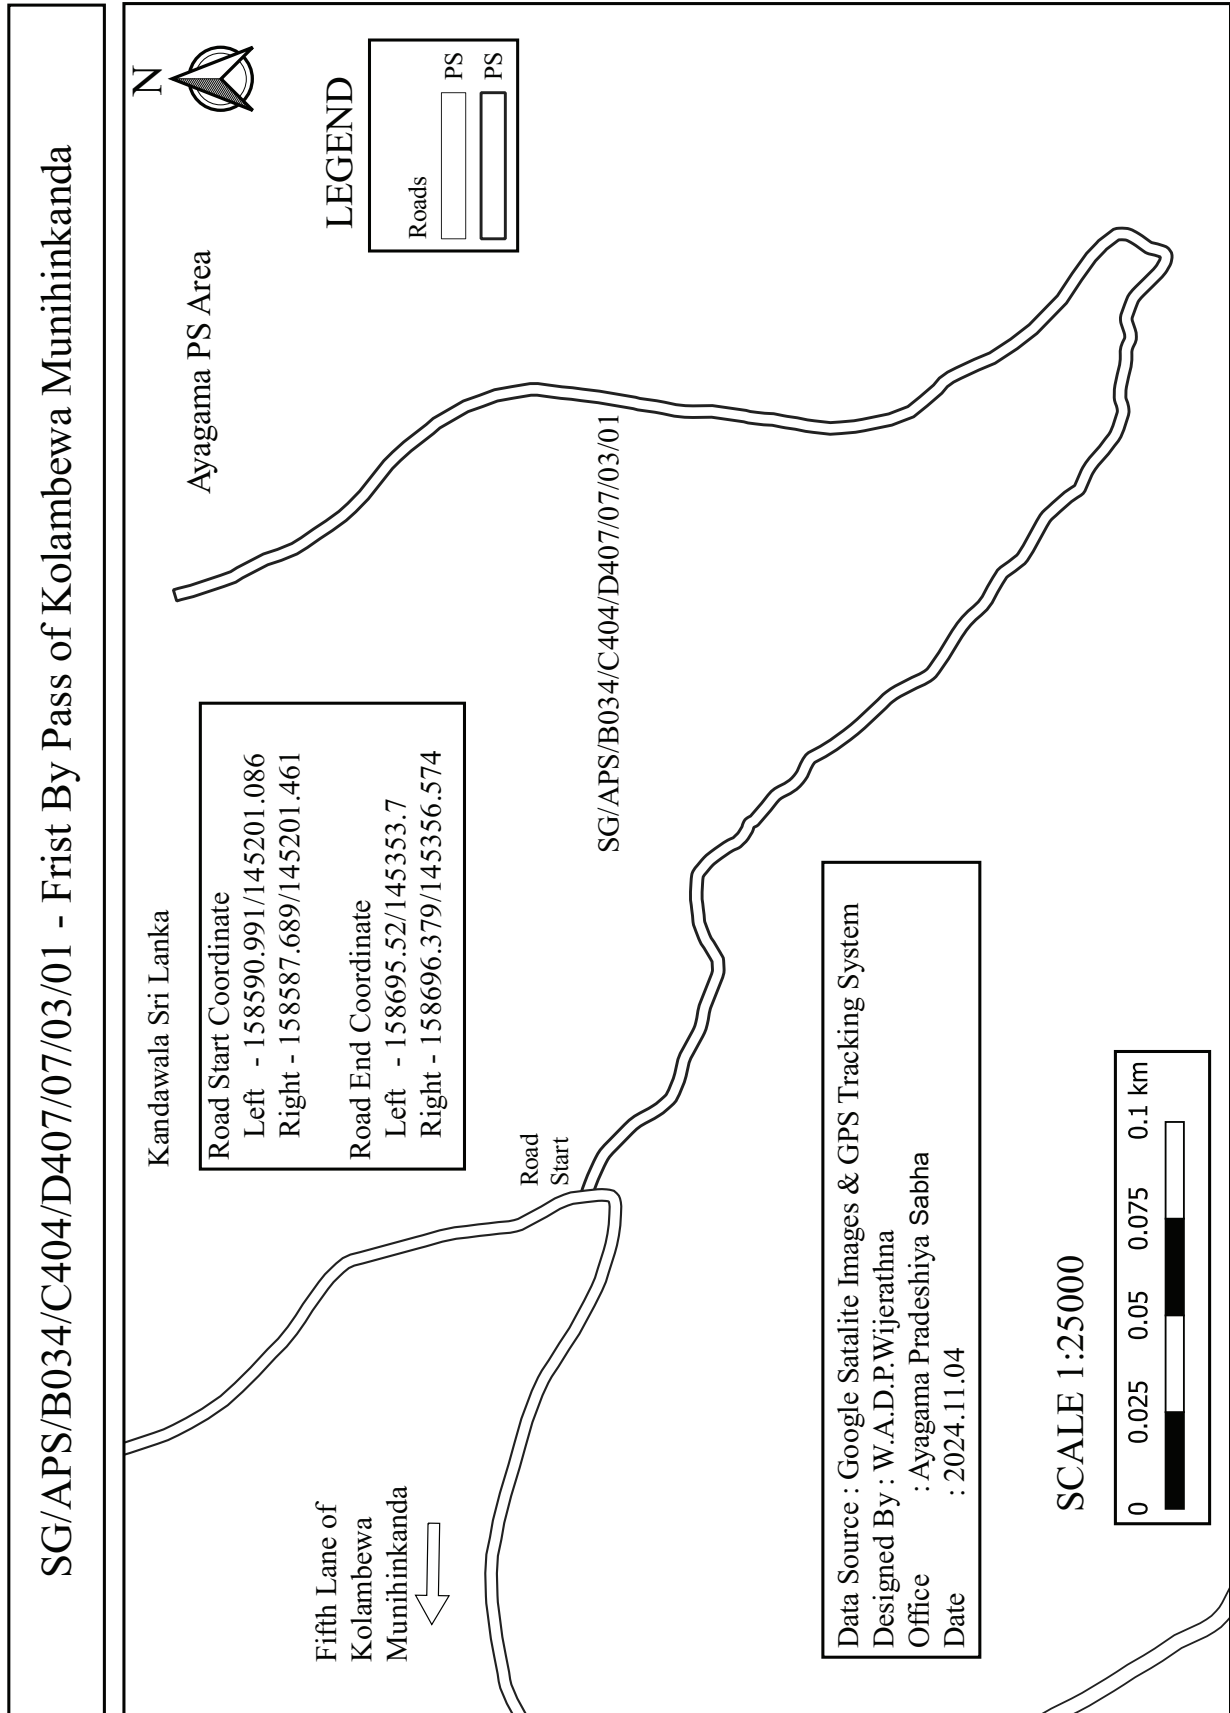


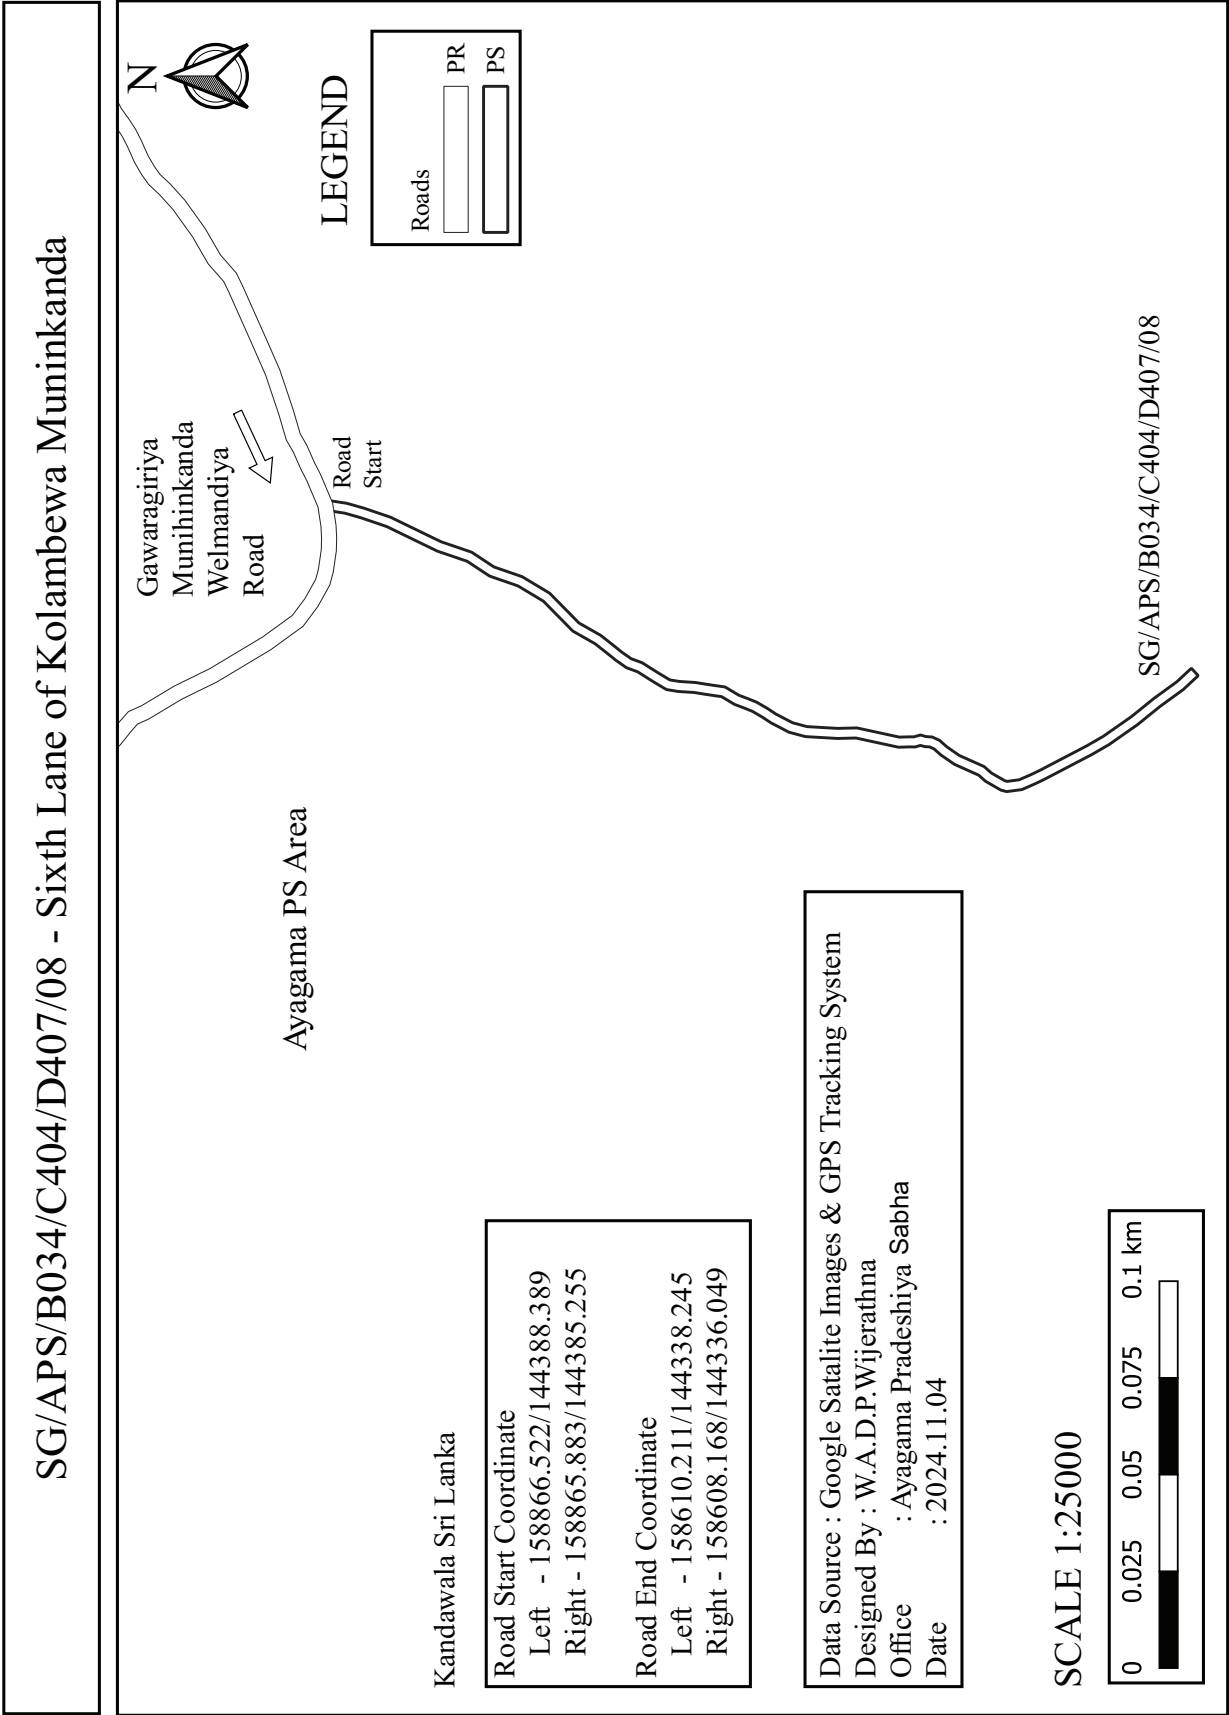


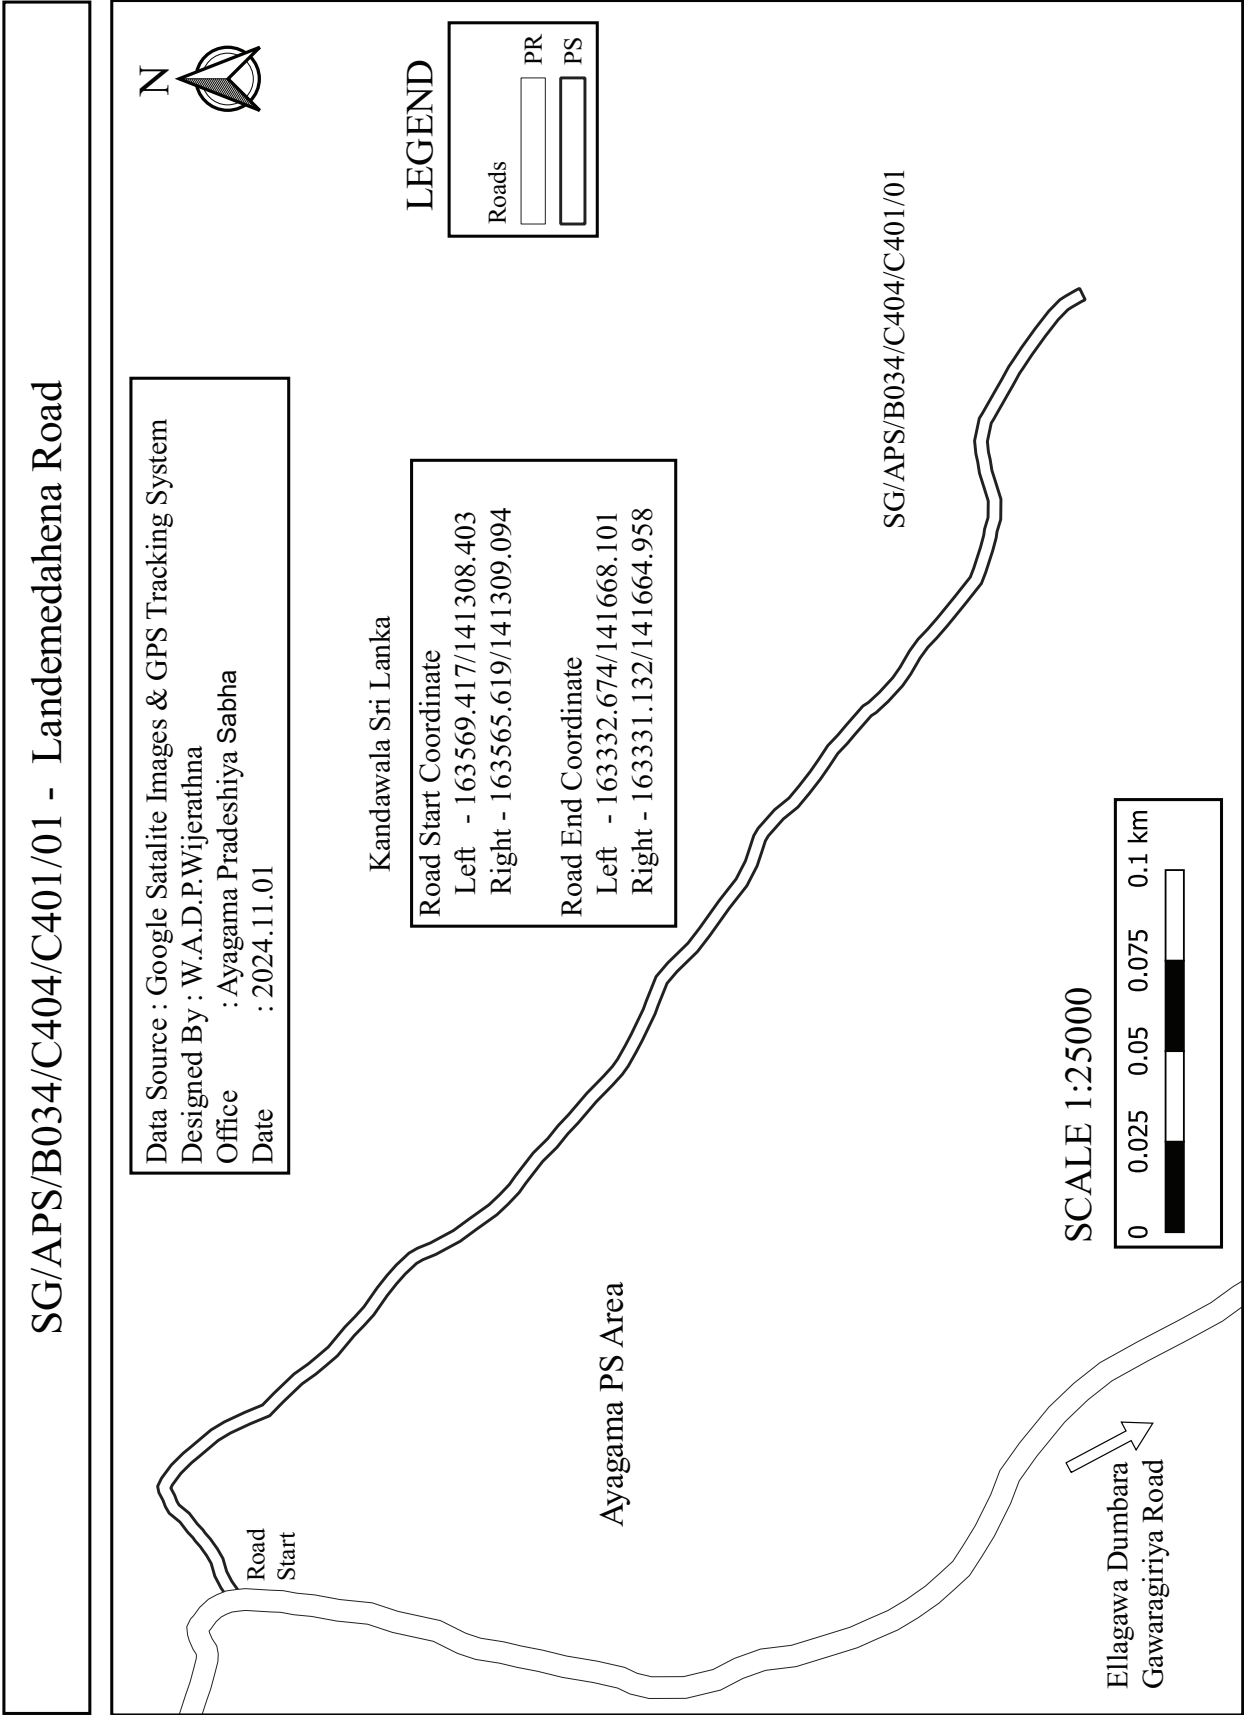


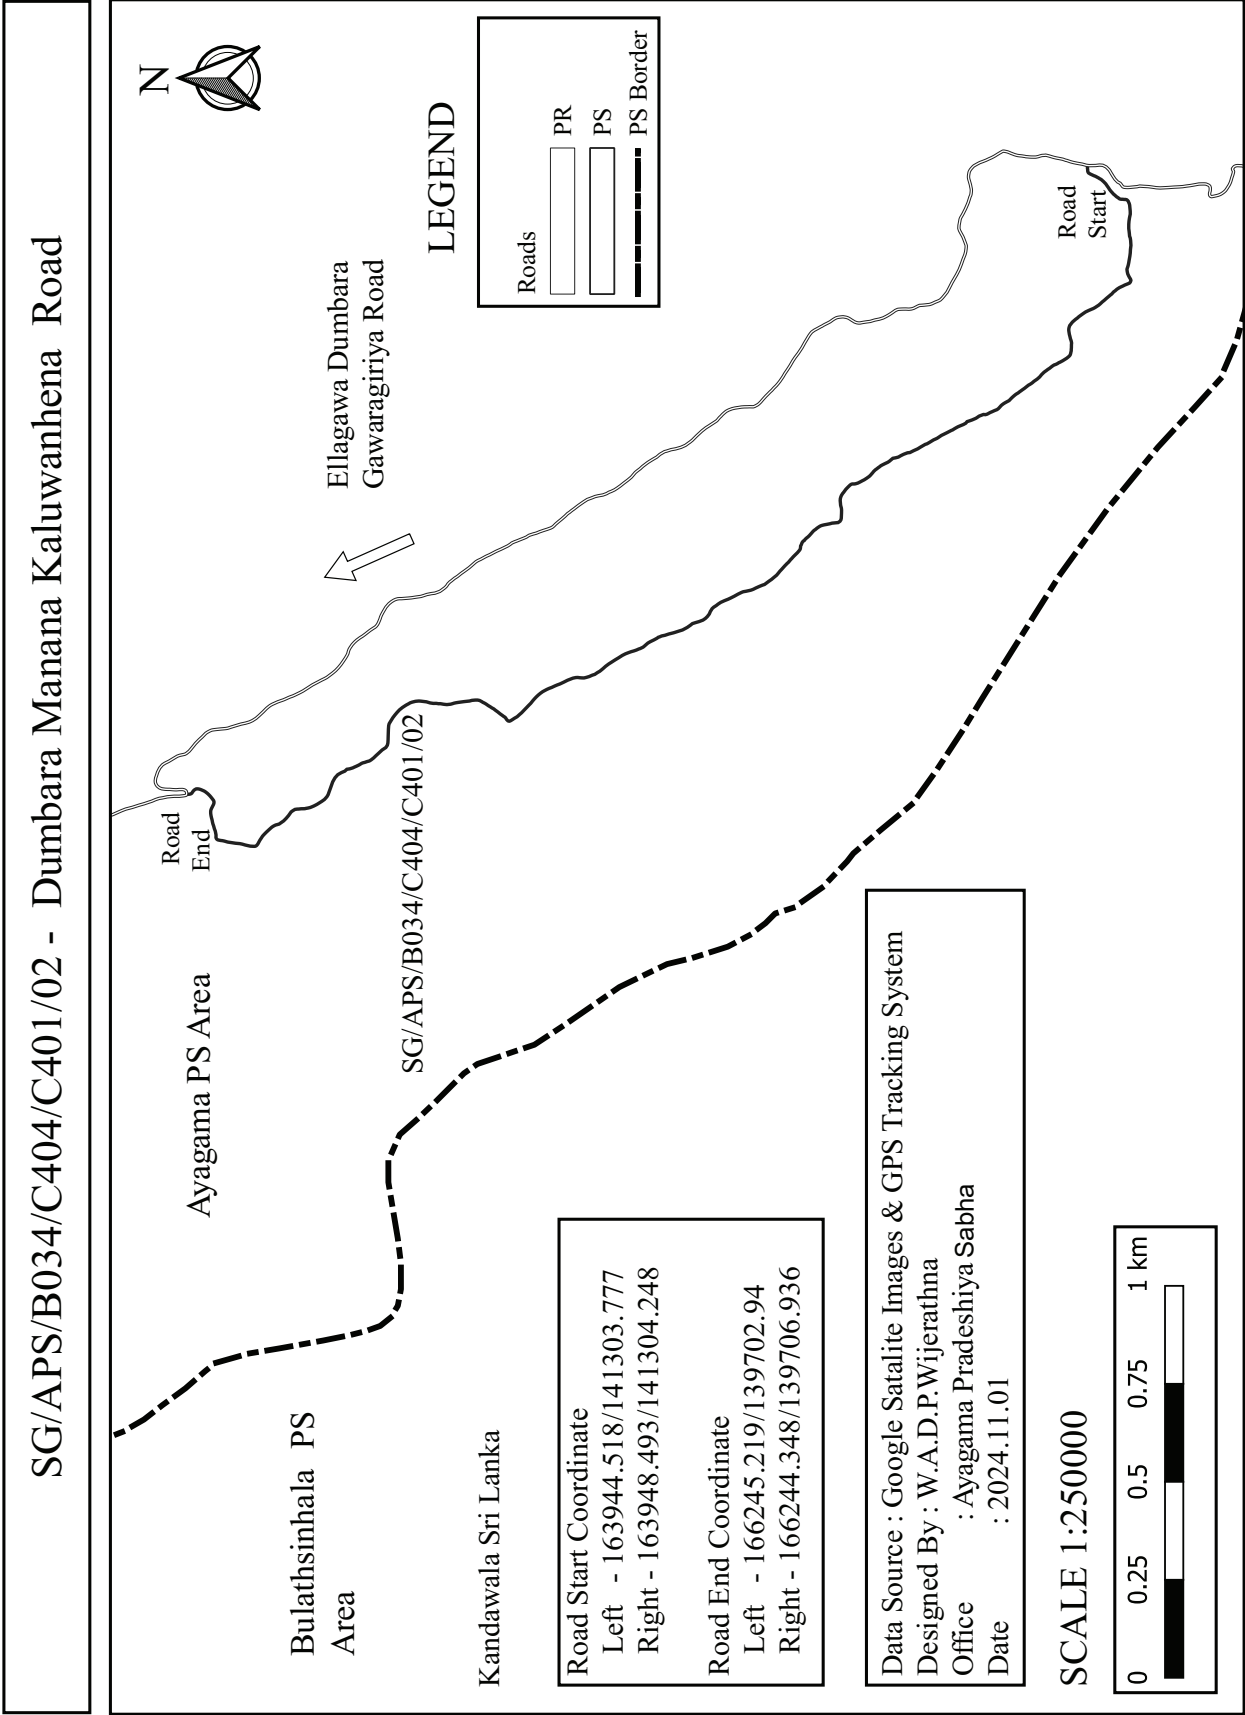


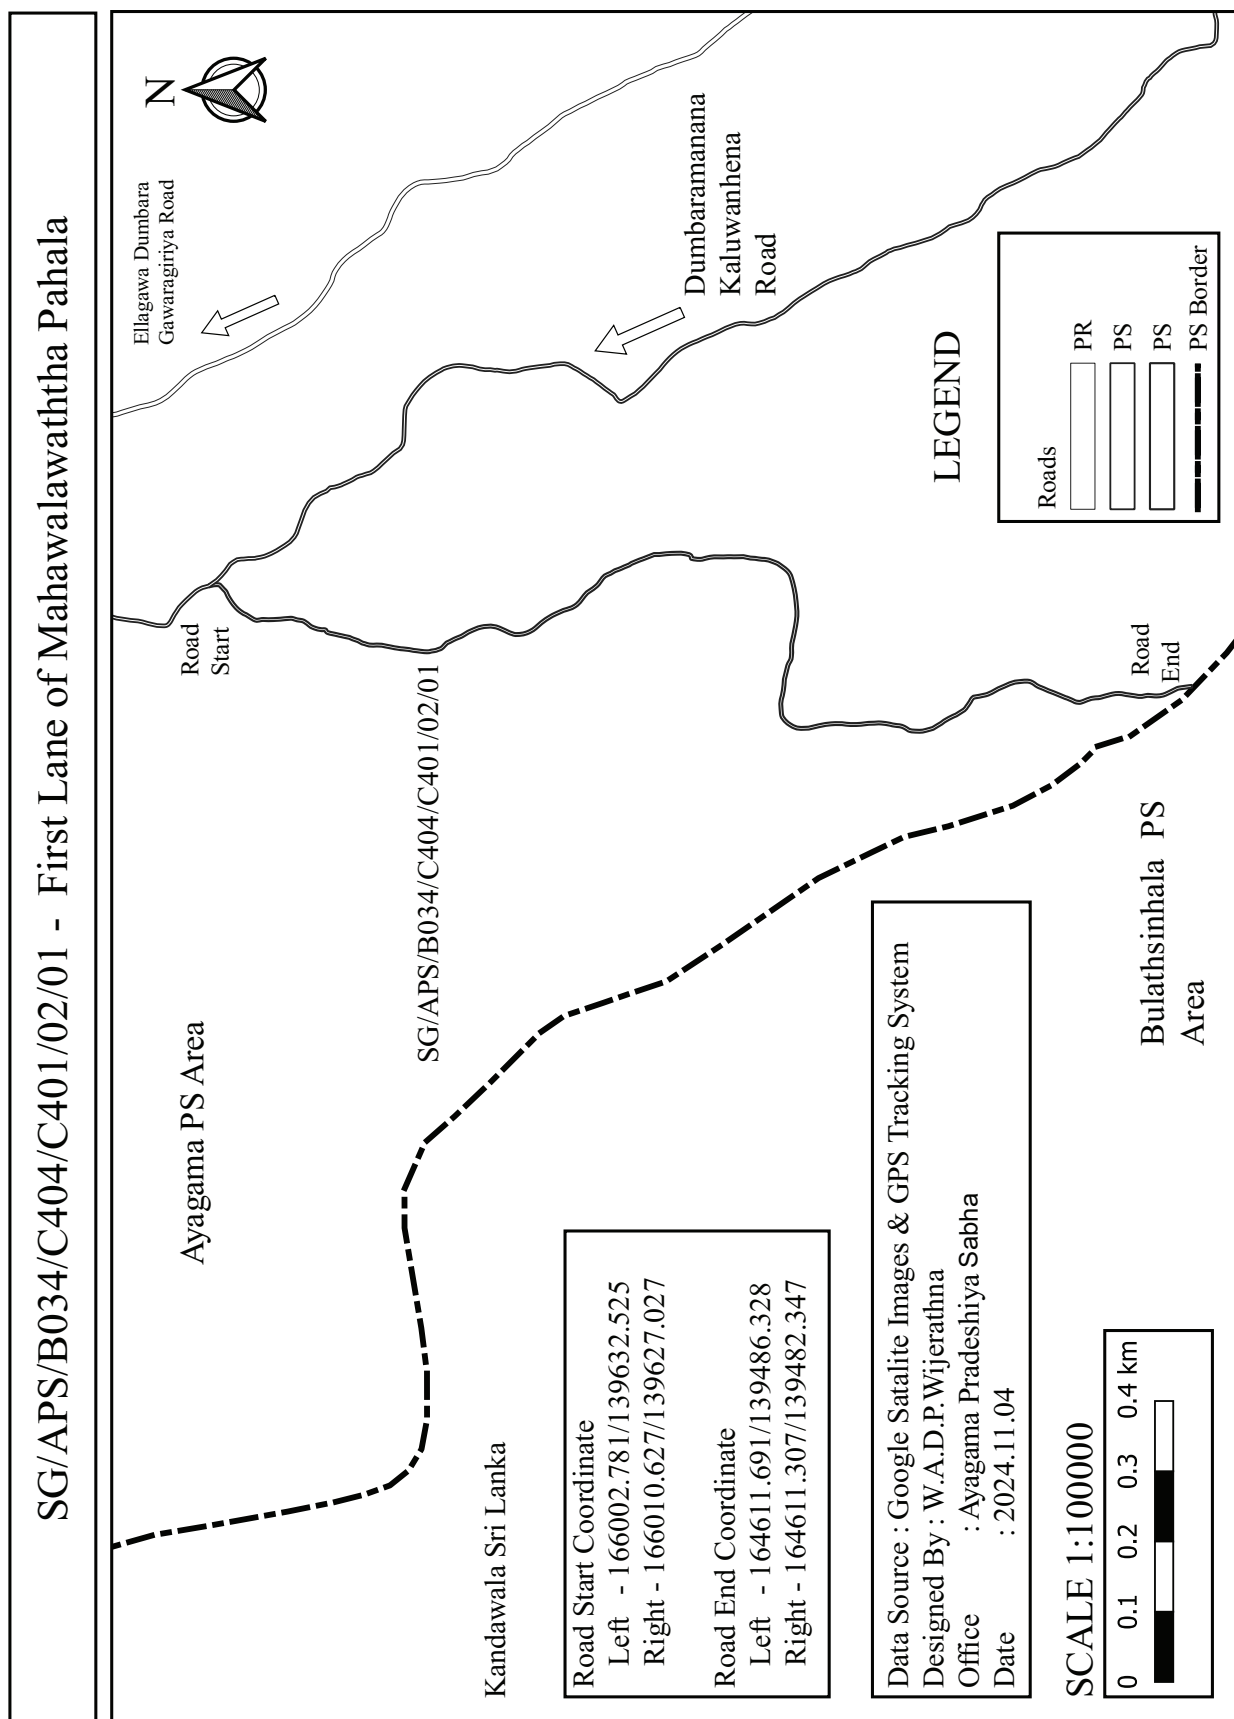


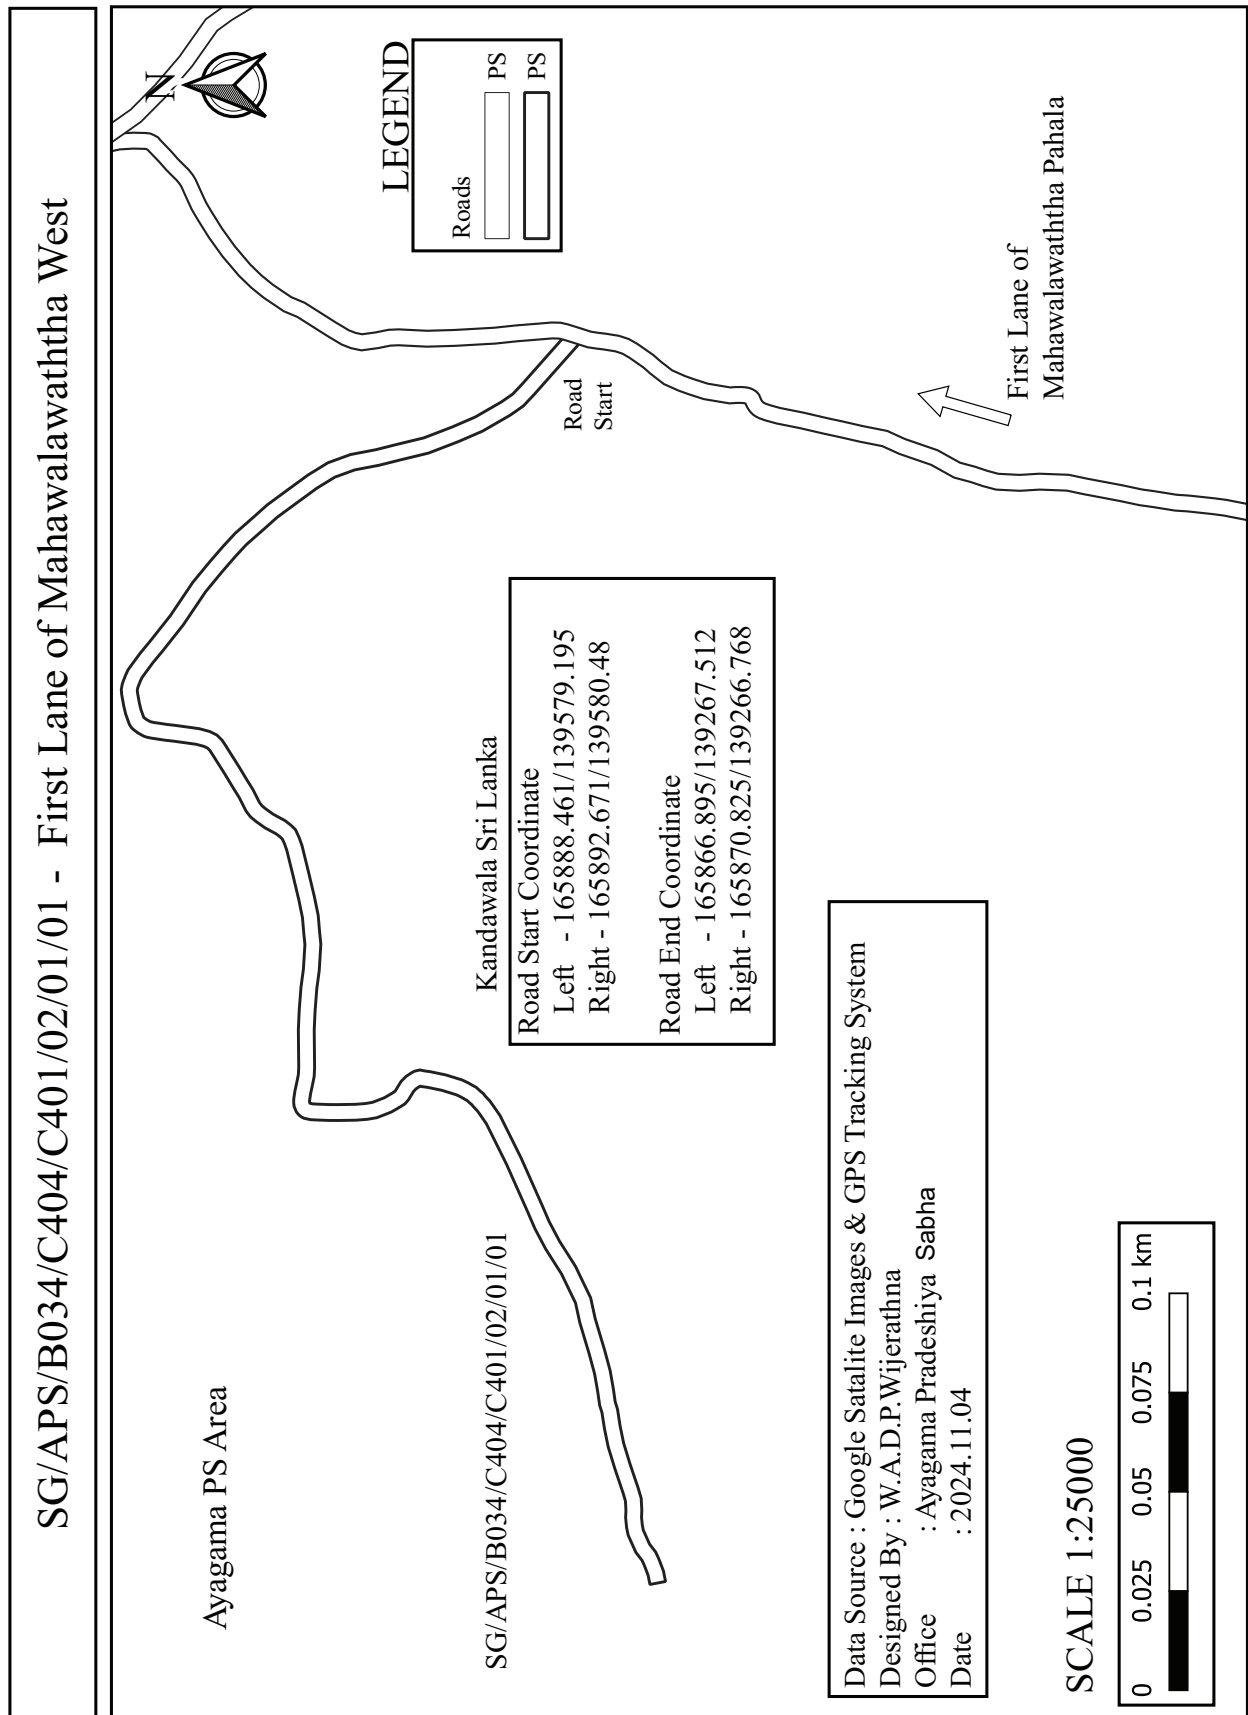

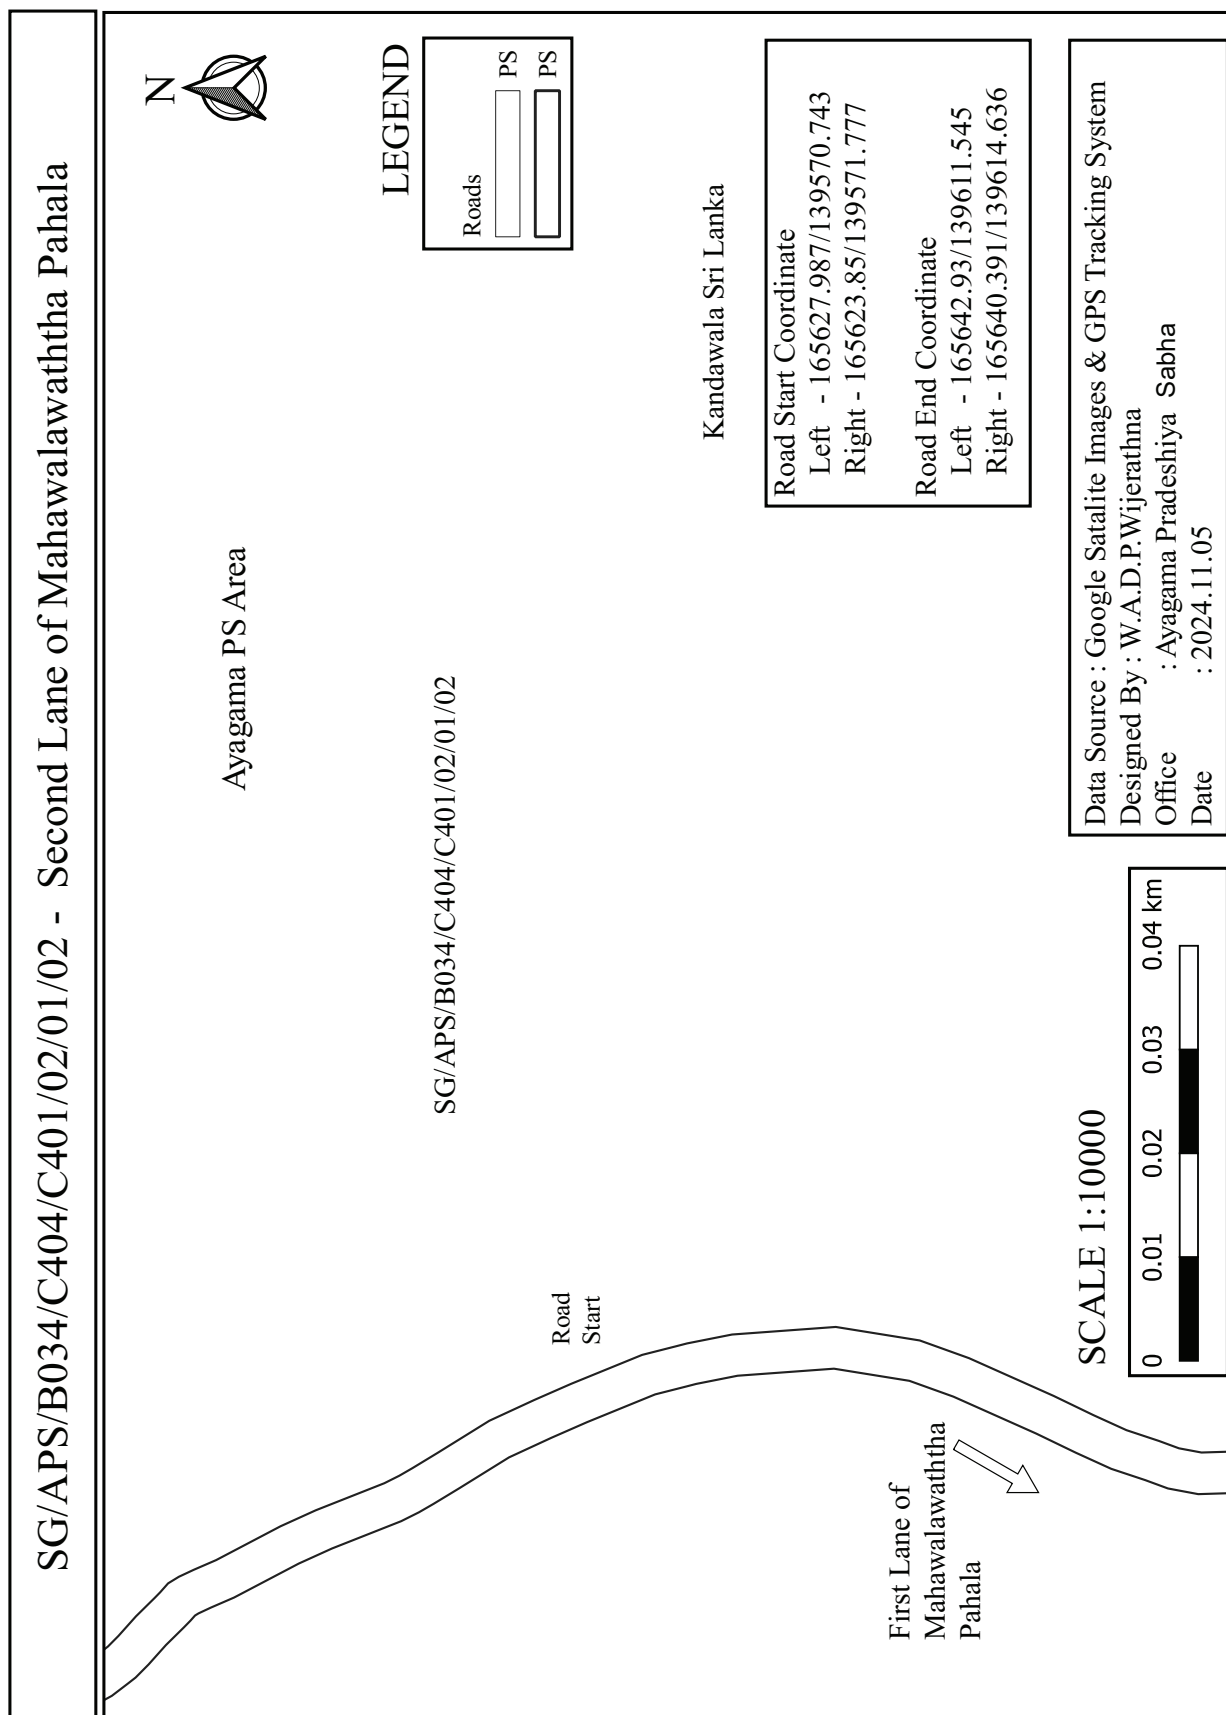


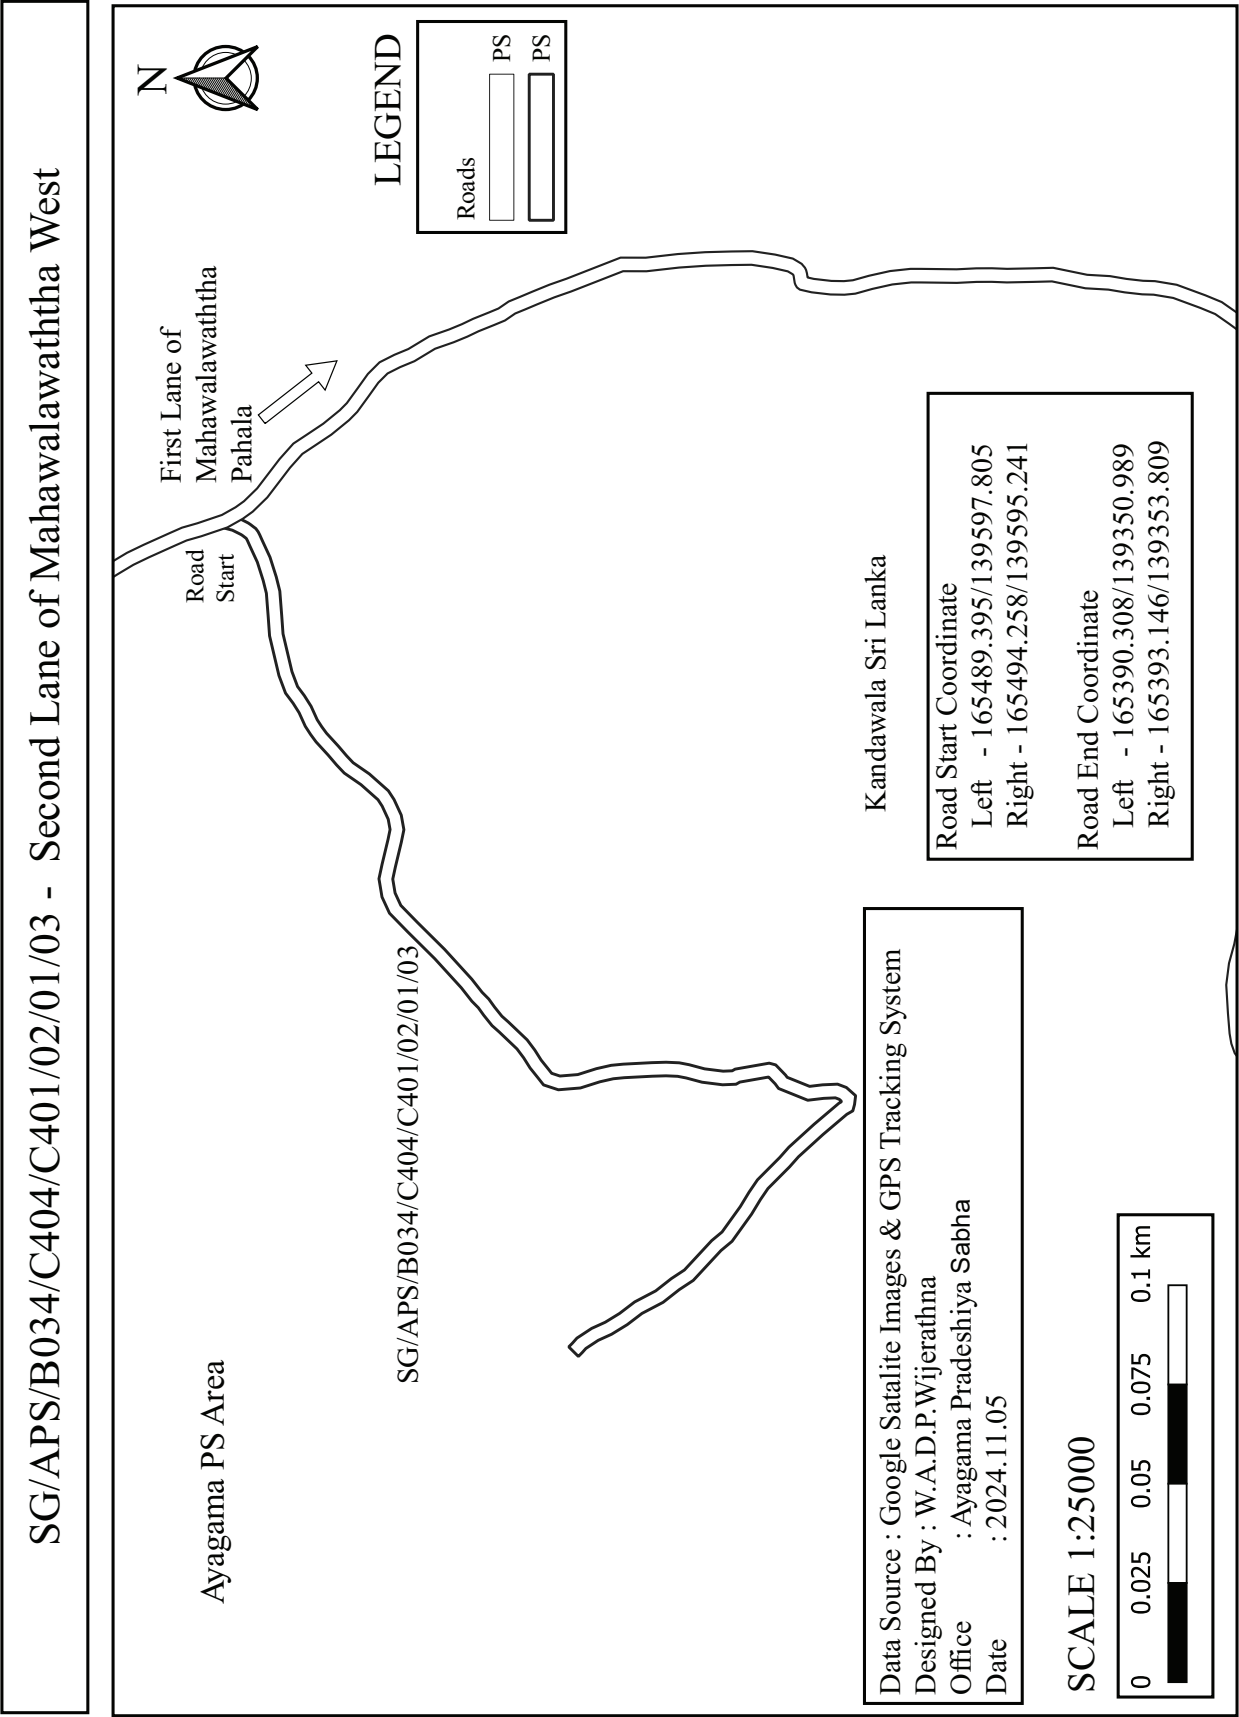

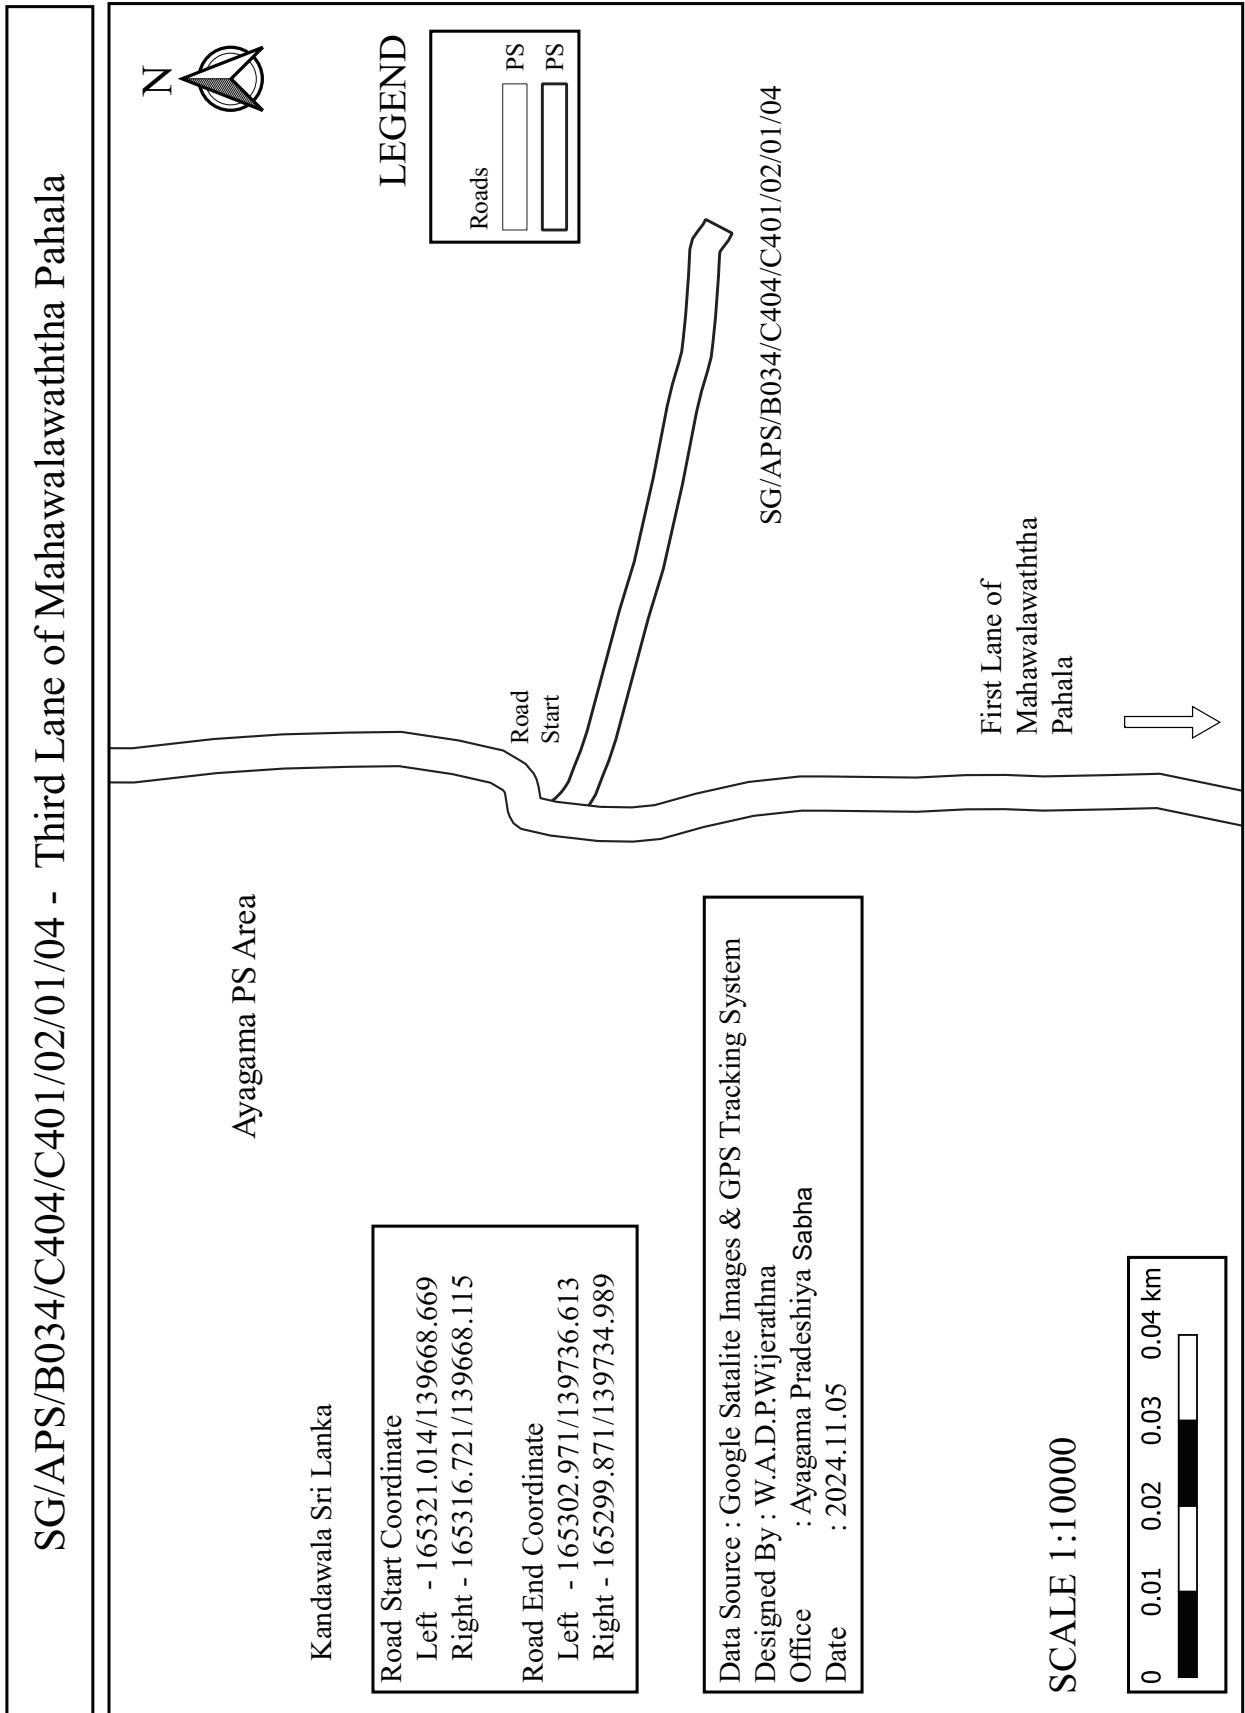


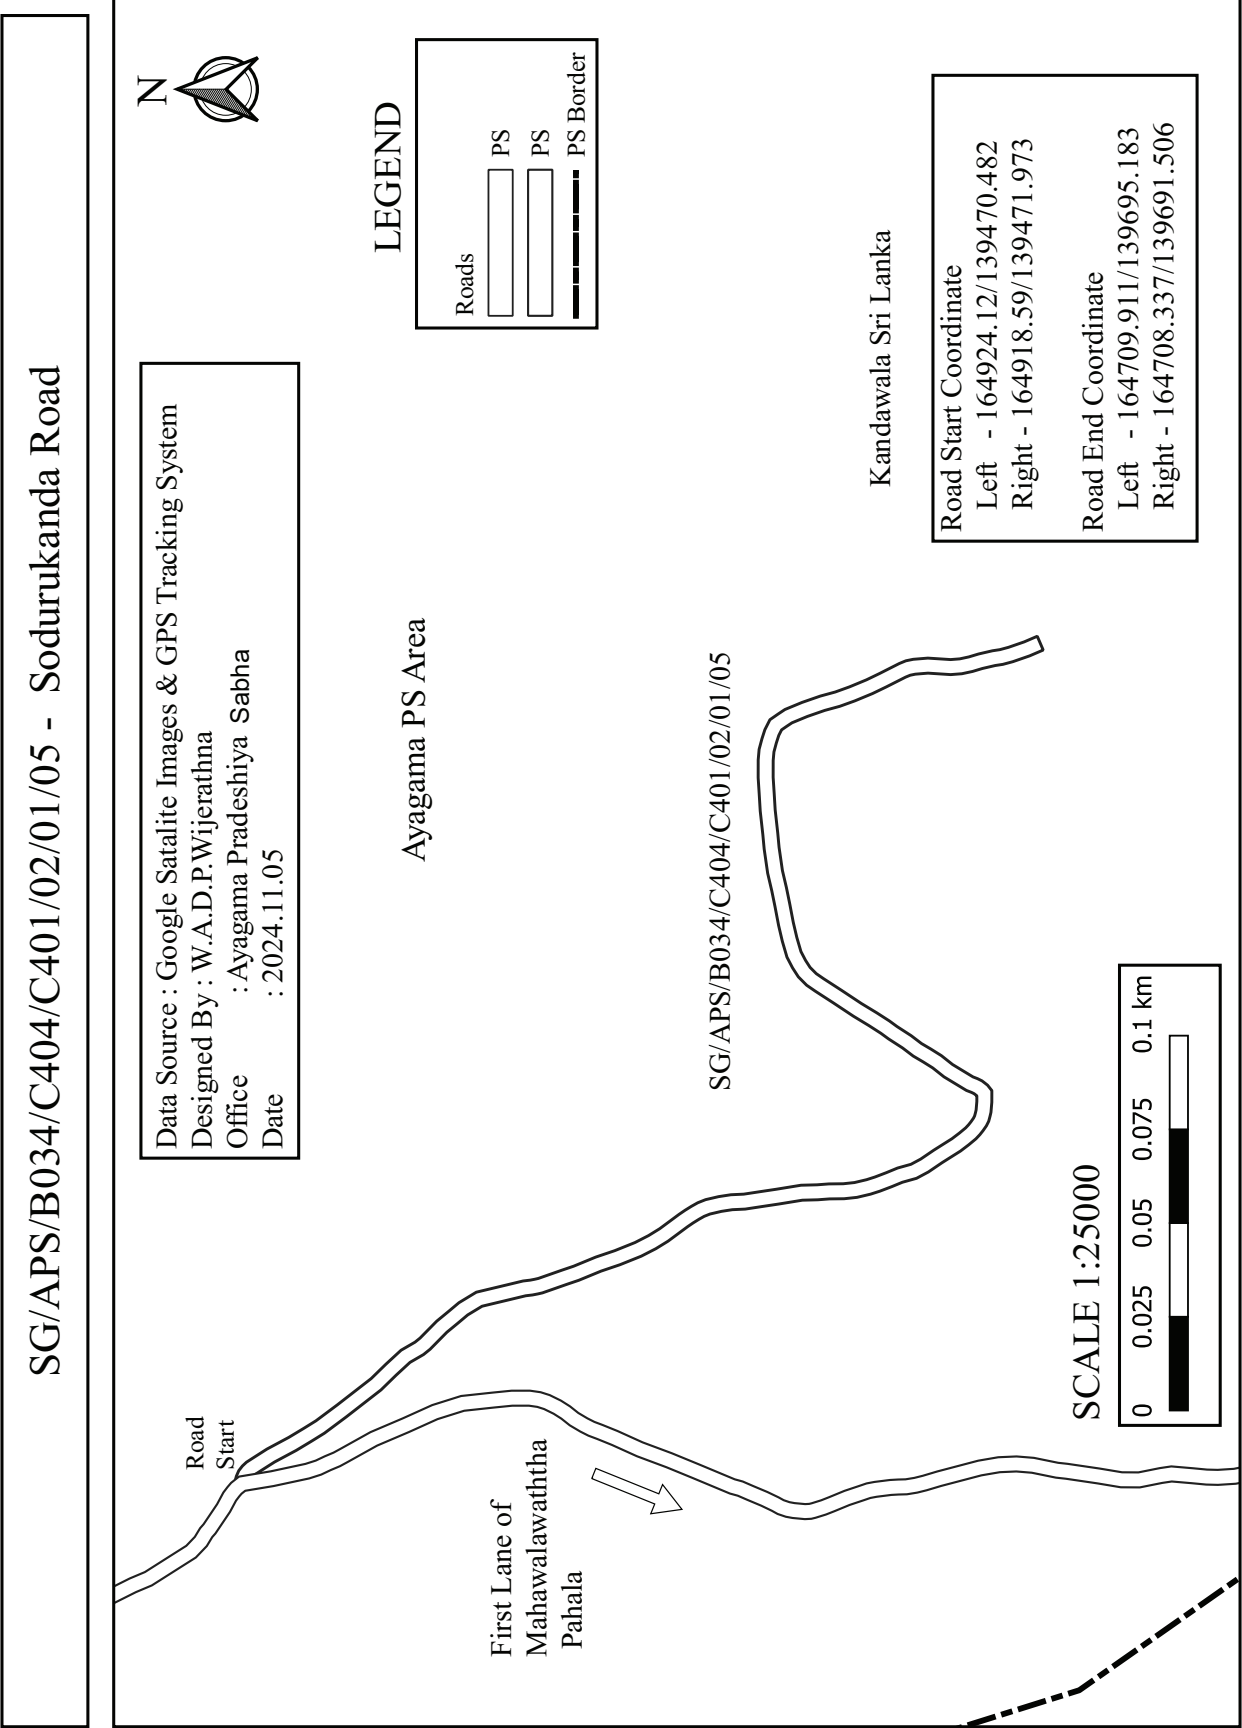


SG/APS/B034/C404/C401/02/02 - Dumbara Road No. 02

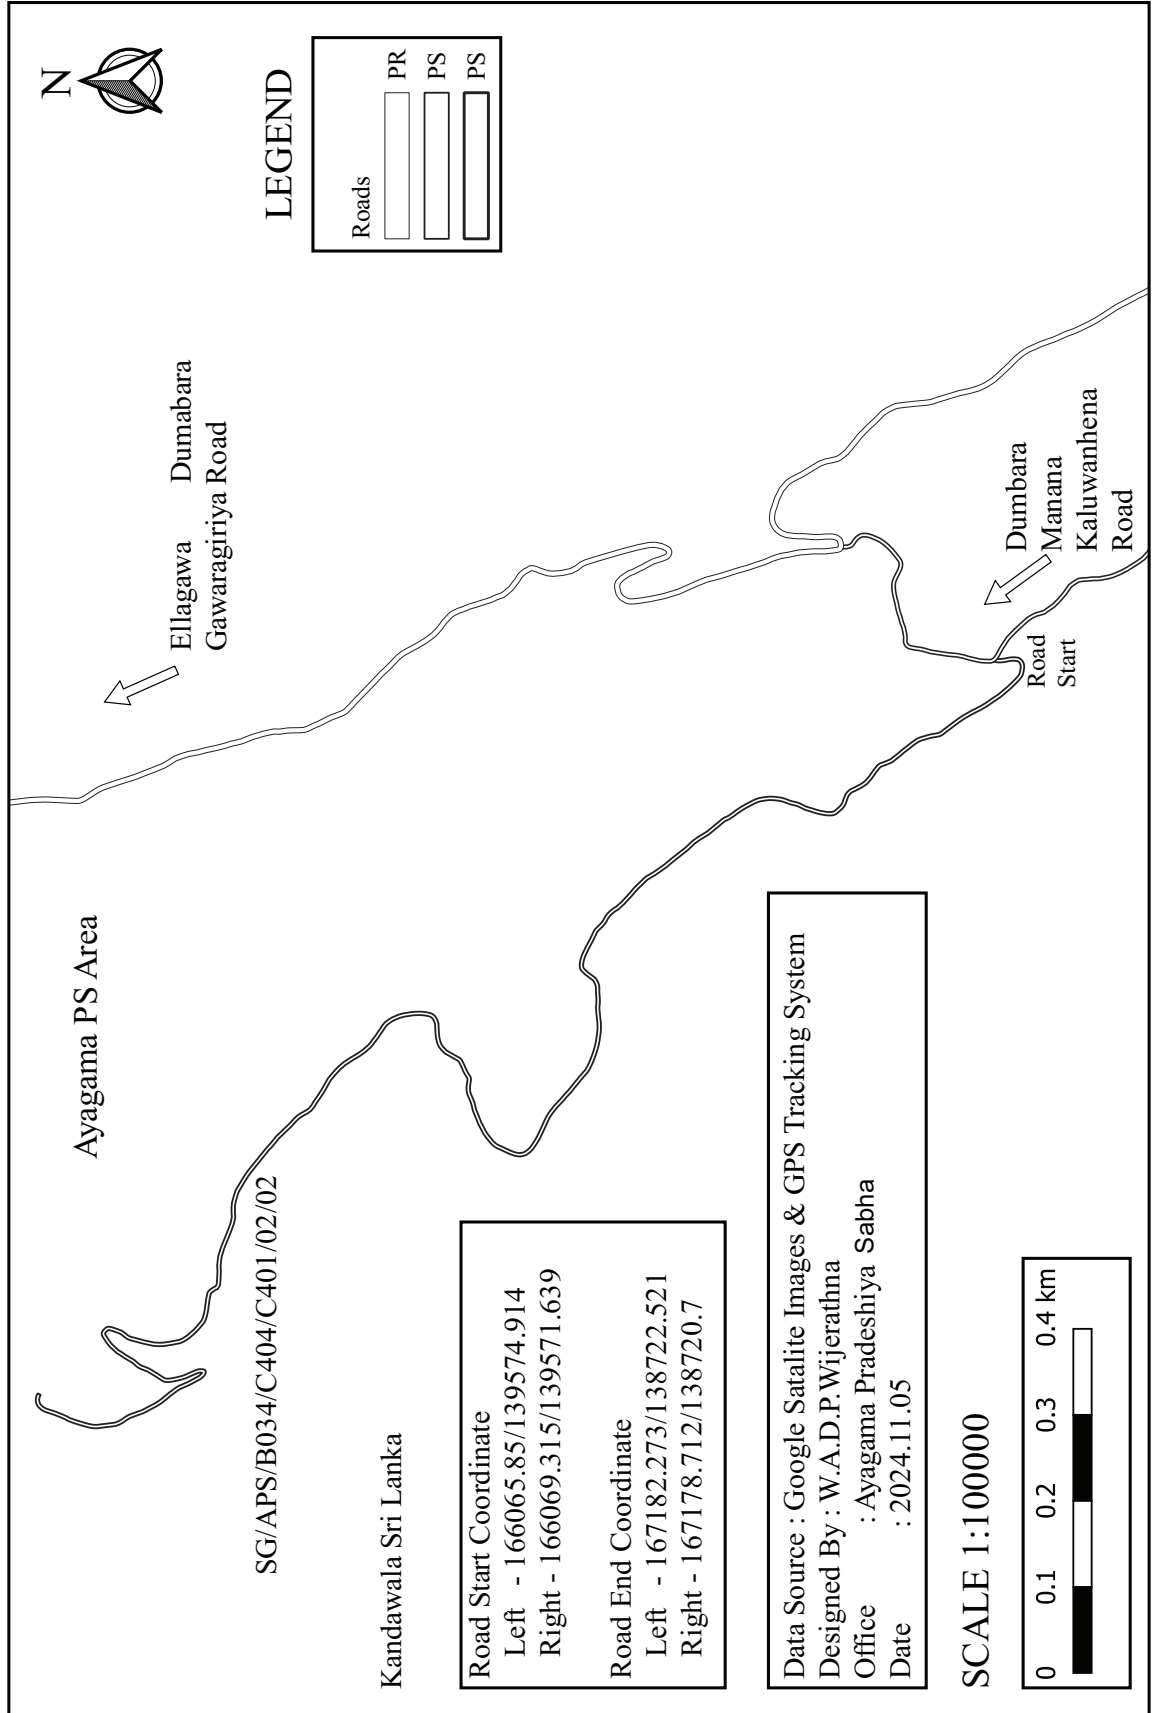


Kandawala Sri Lanka

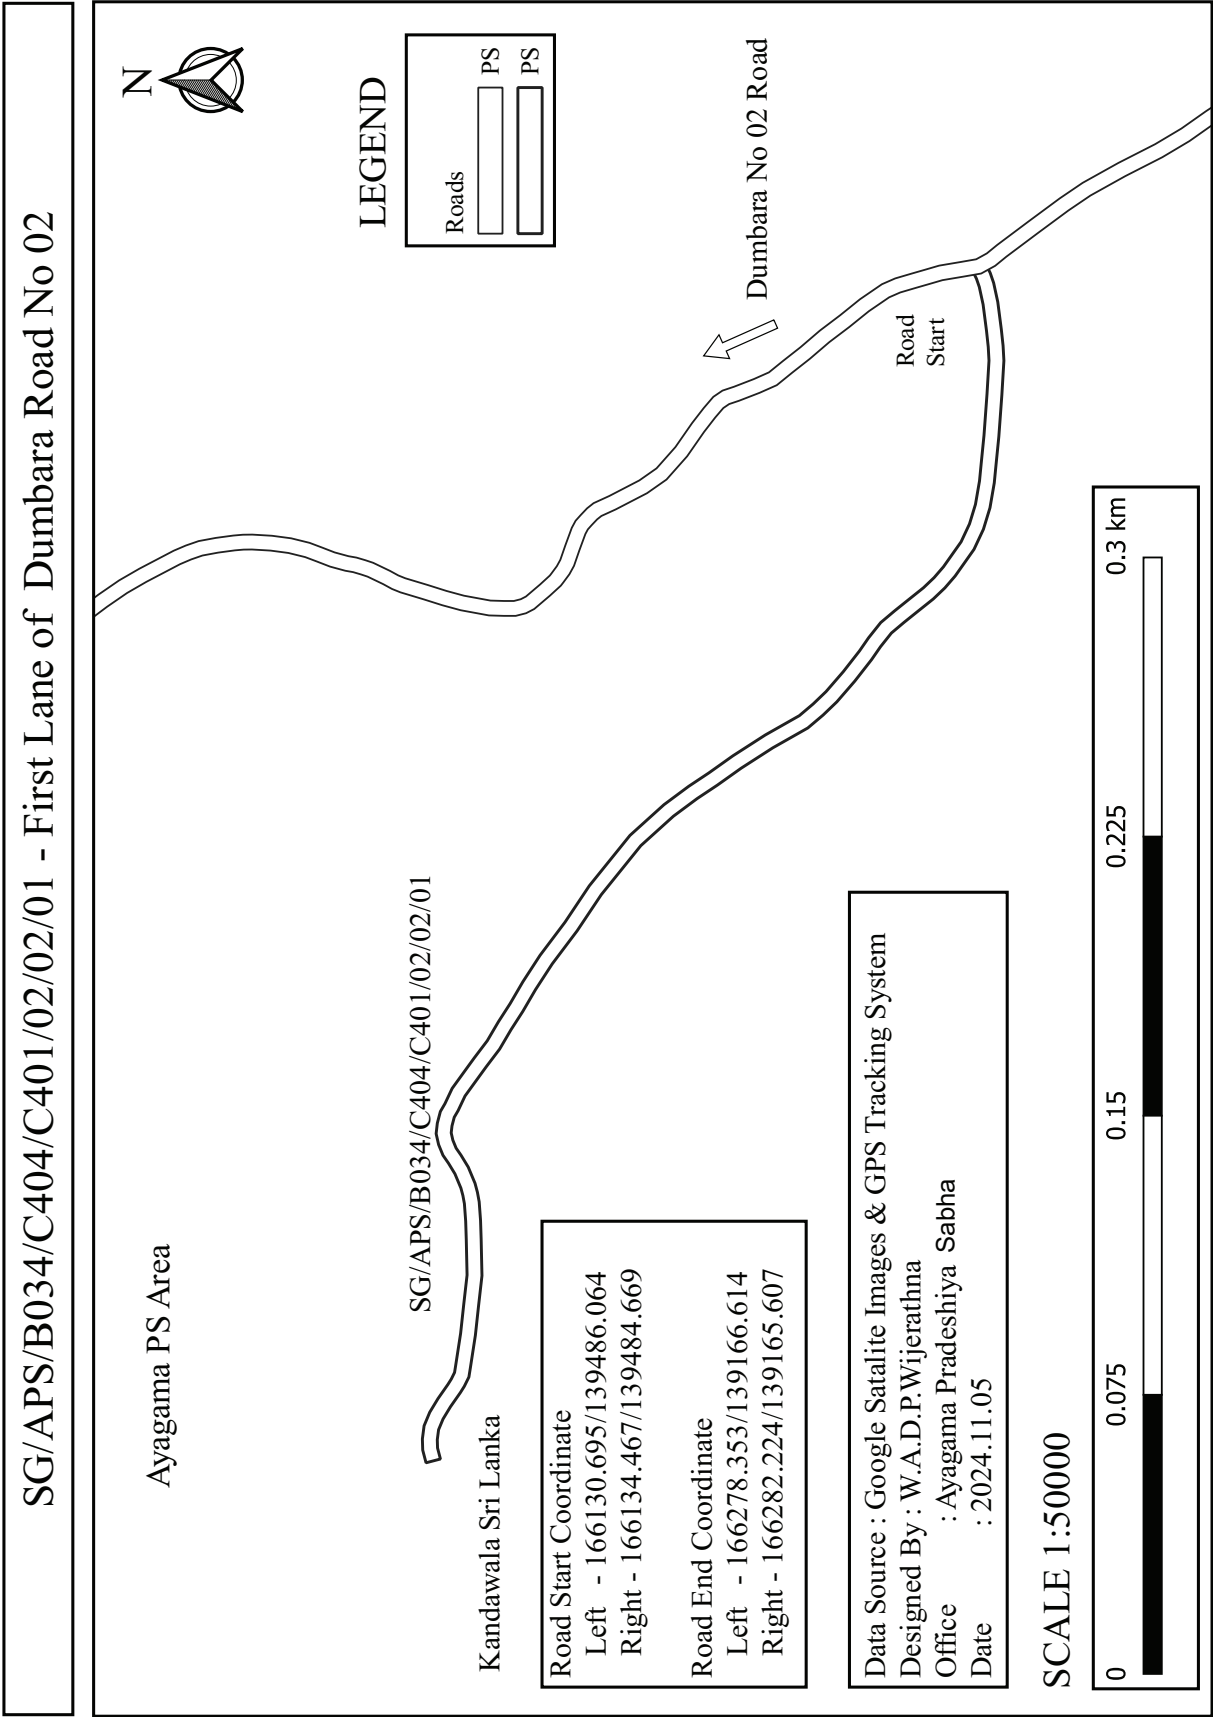


SG/APS/B034/C404/C401/02/02/01/01 - First By Pass of the First Lane of Dumbara Road No 02

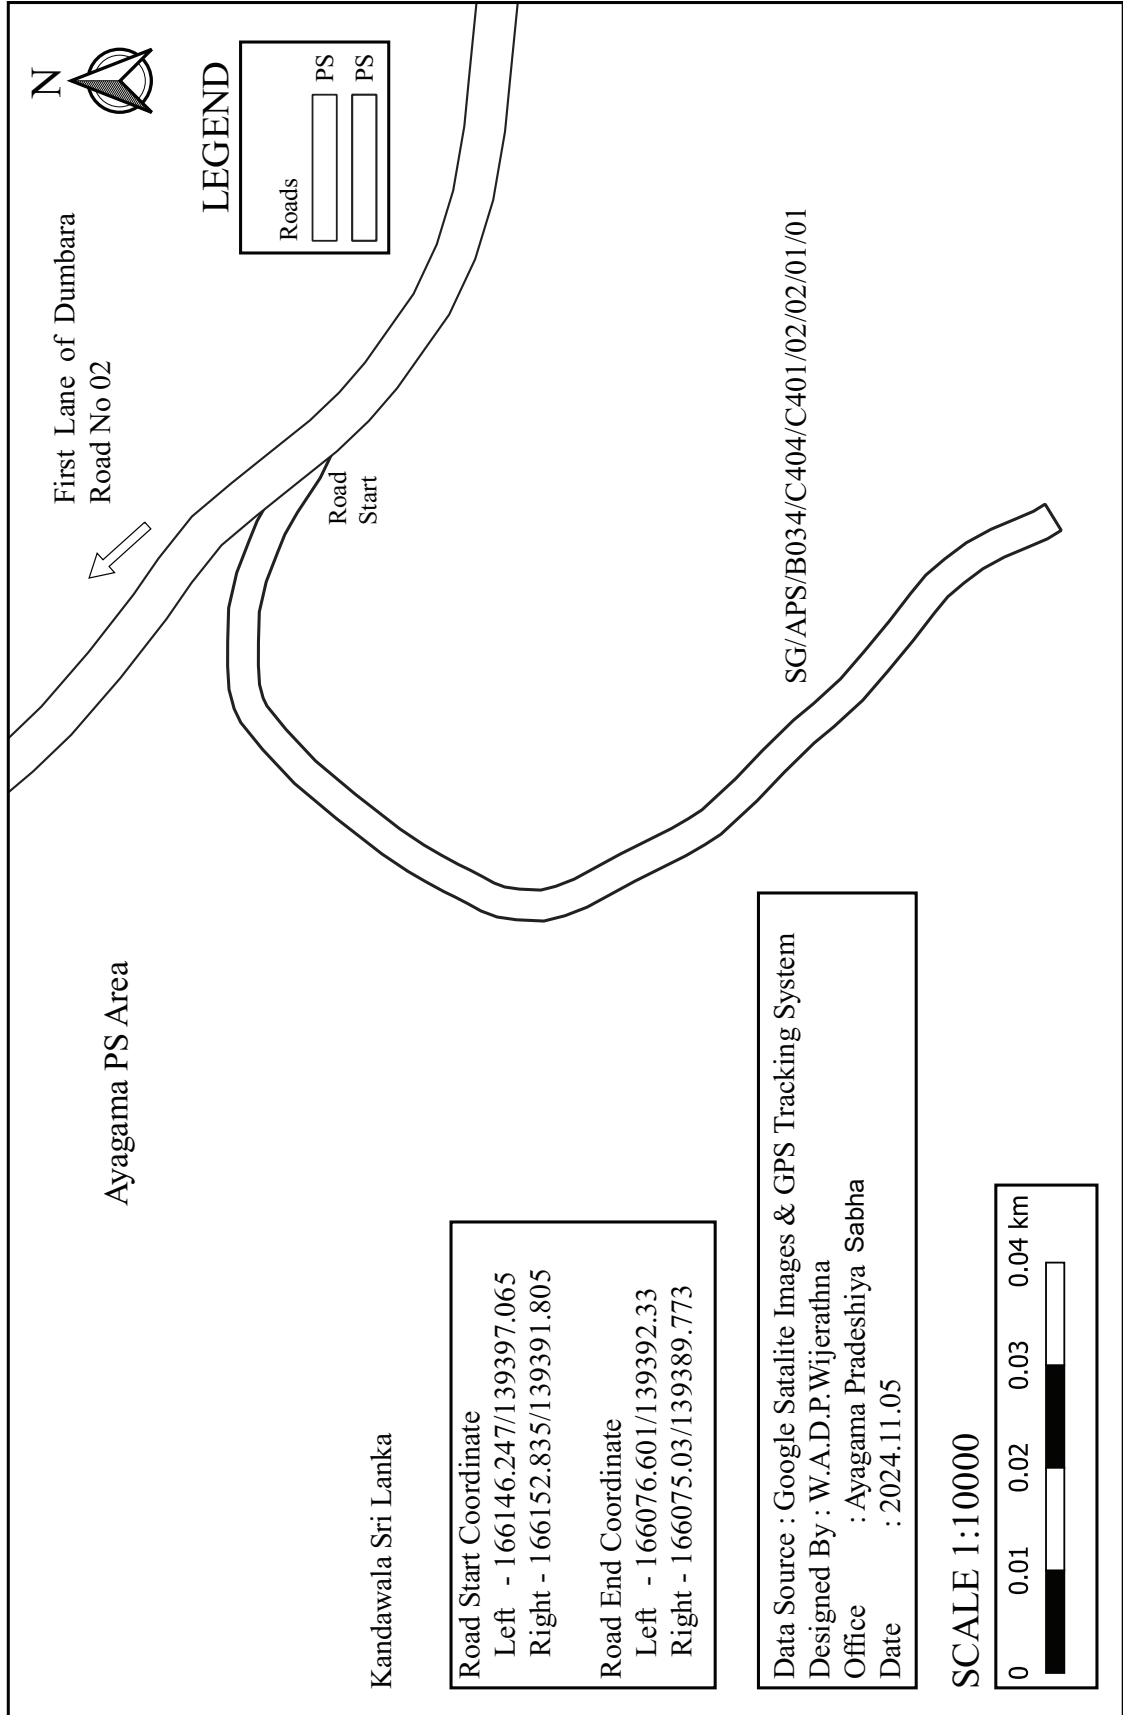


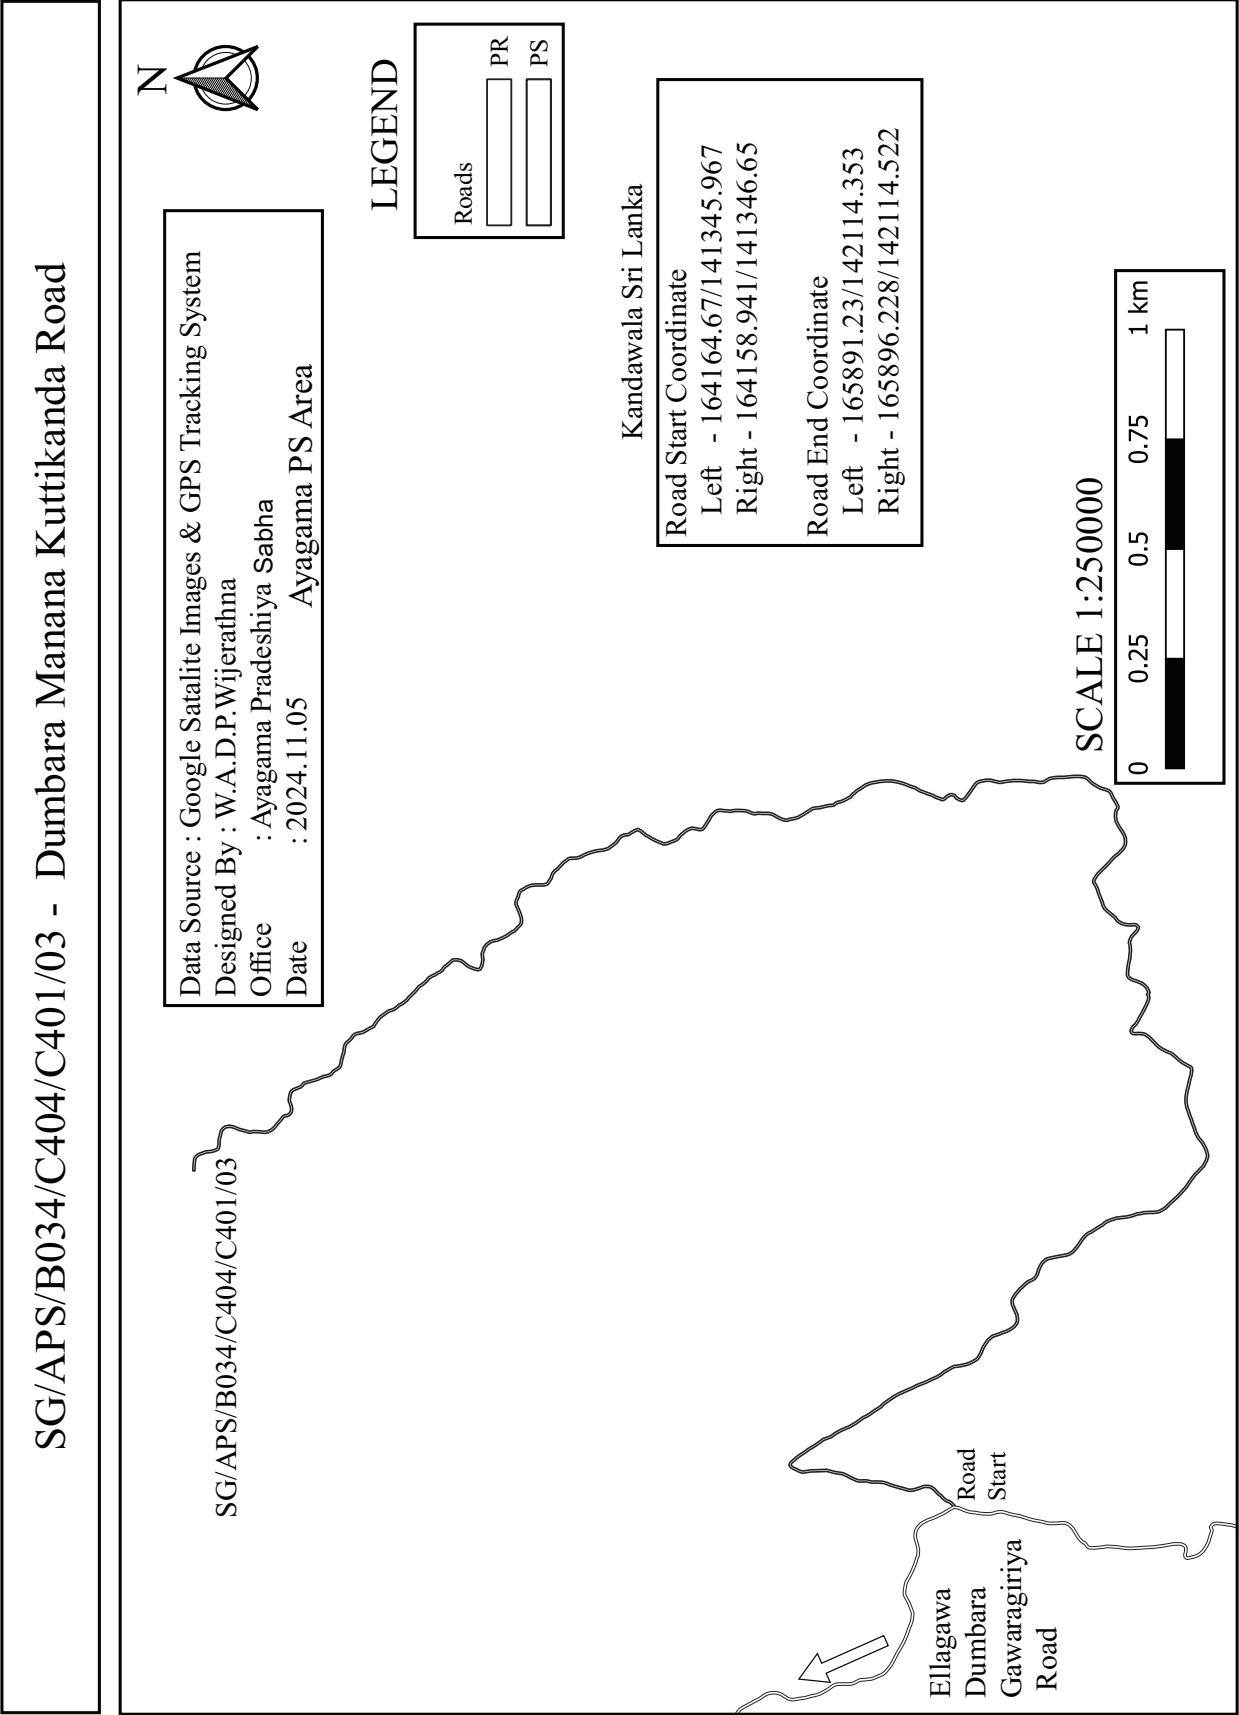



SG/APS/B034/C404/C401/03/01 - No. 01 Dumbara Manana Road

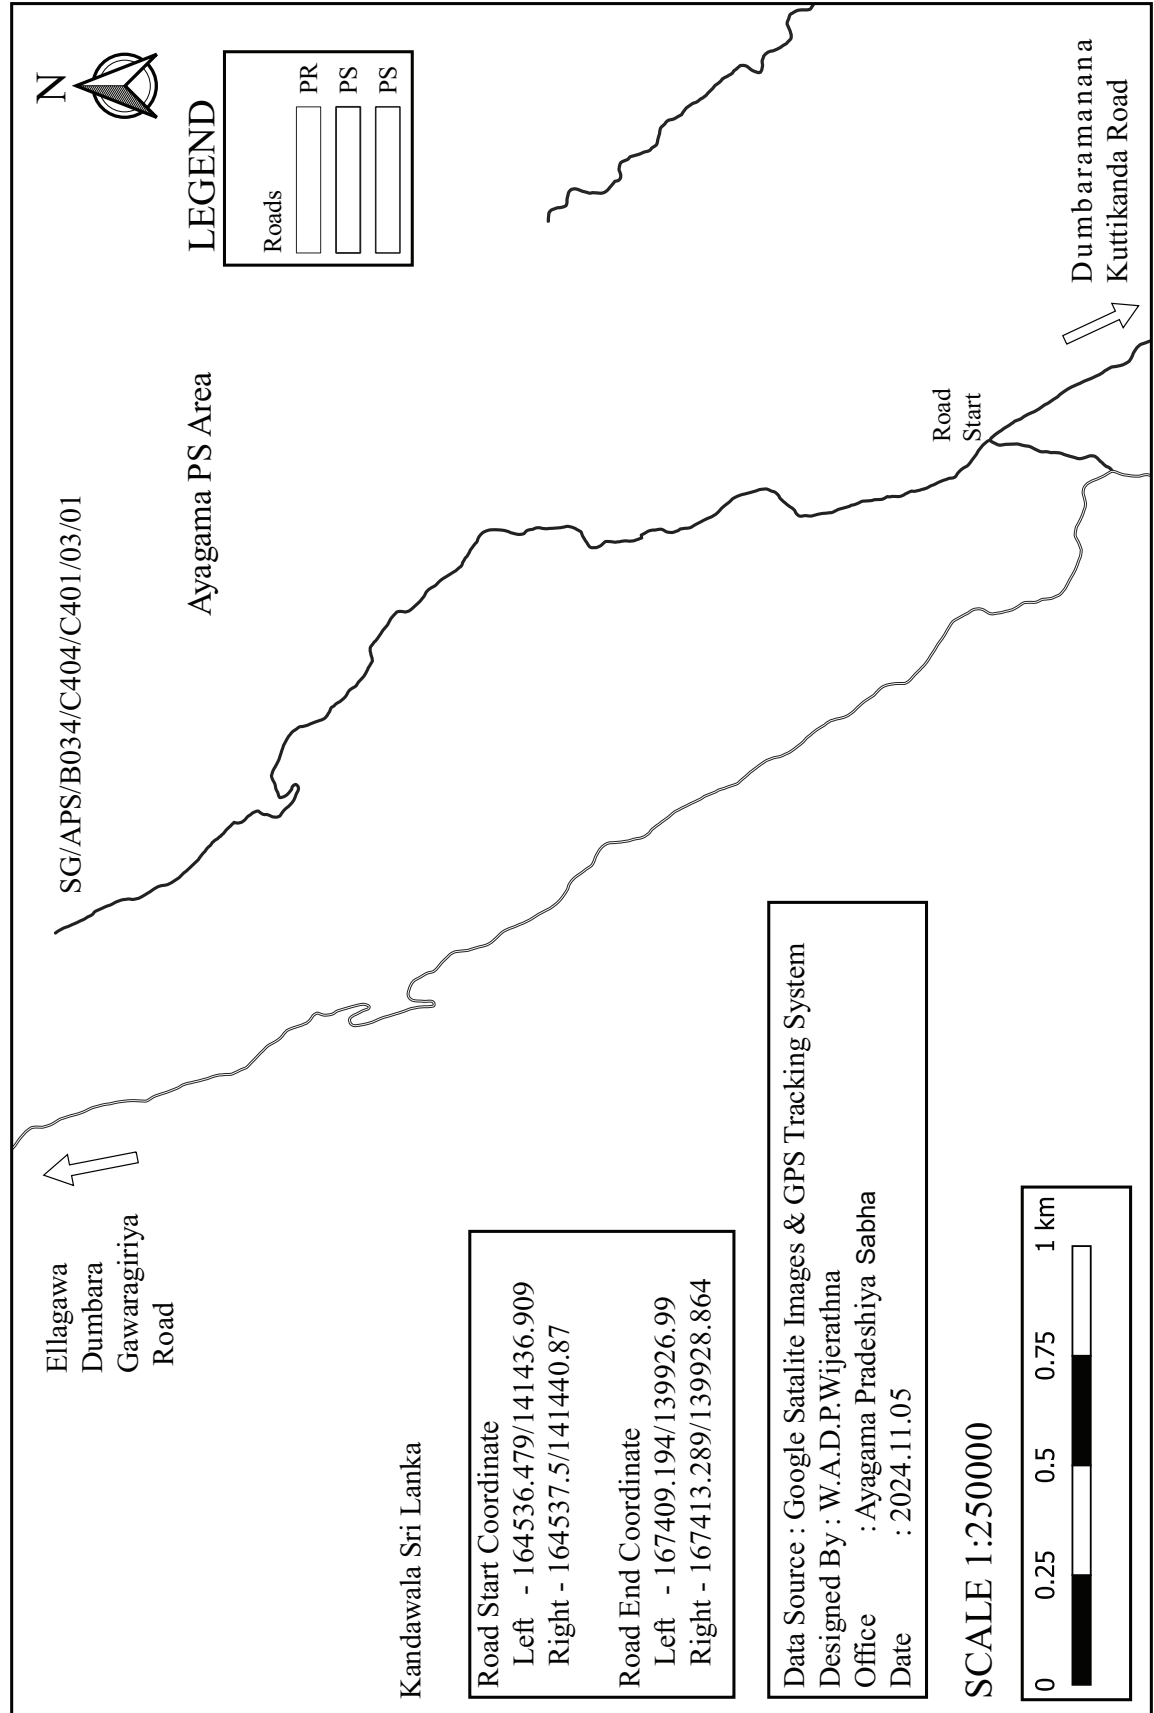




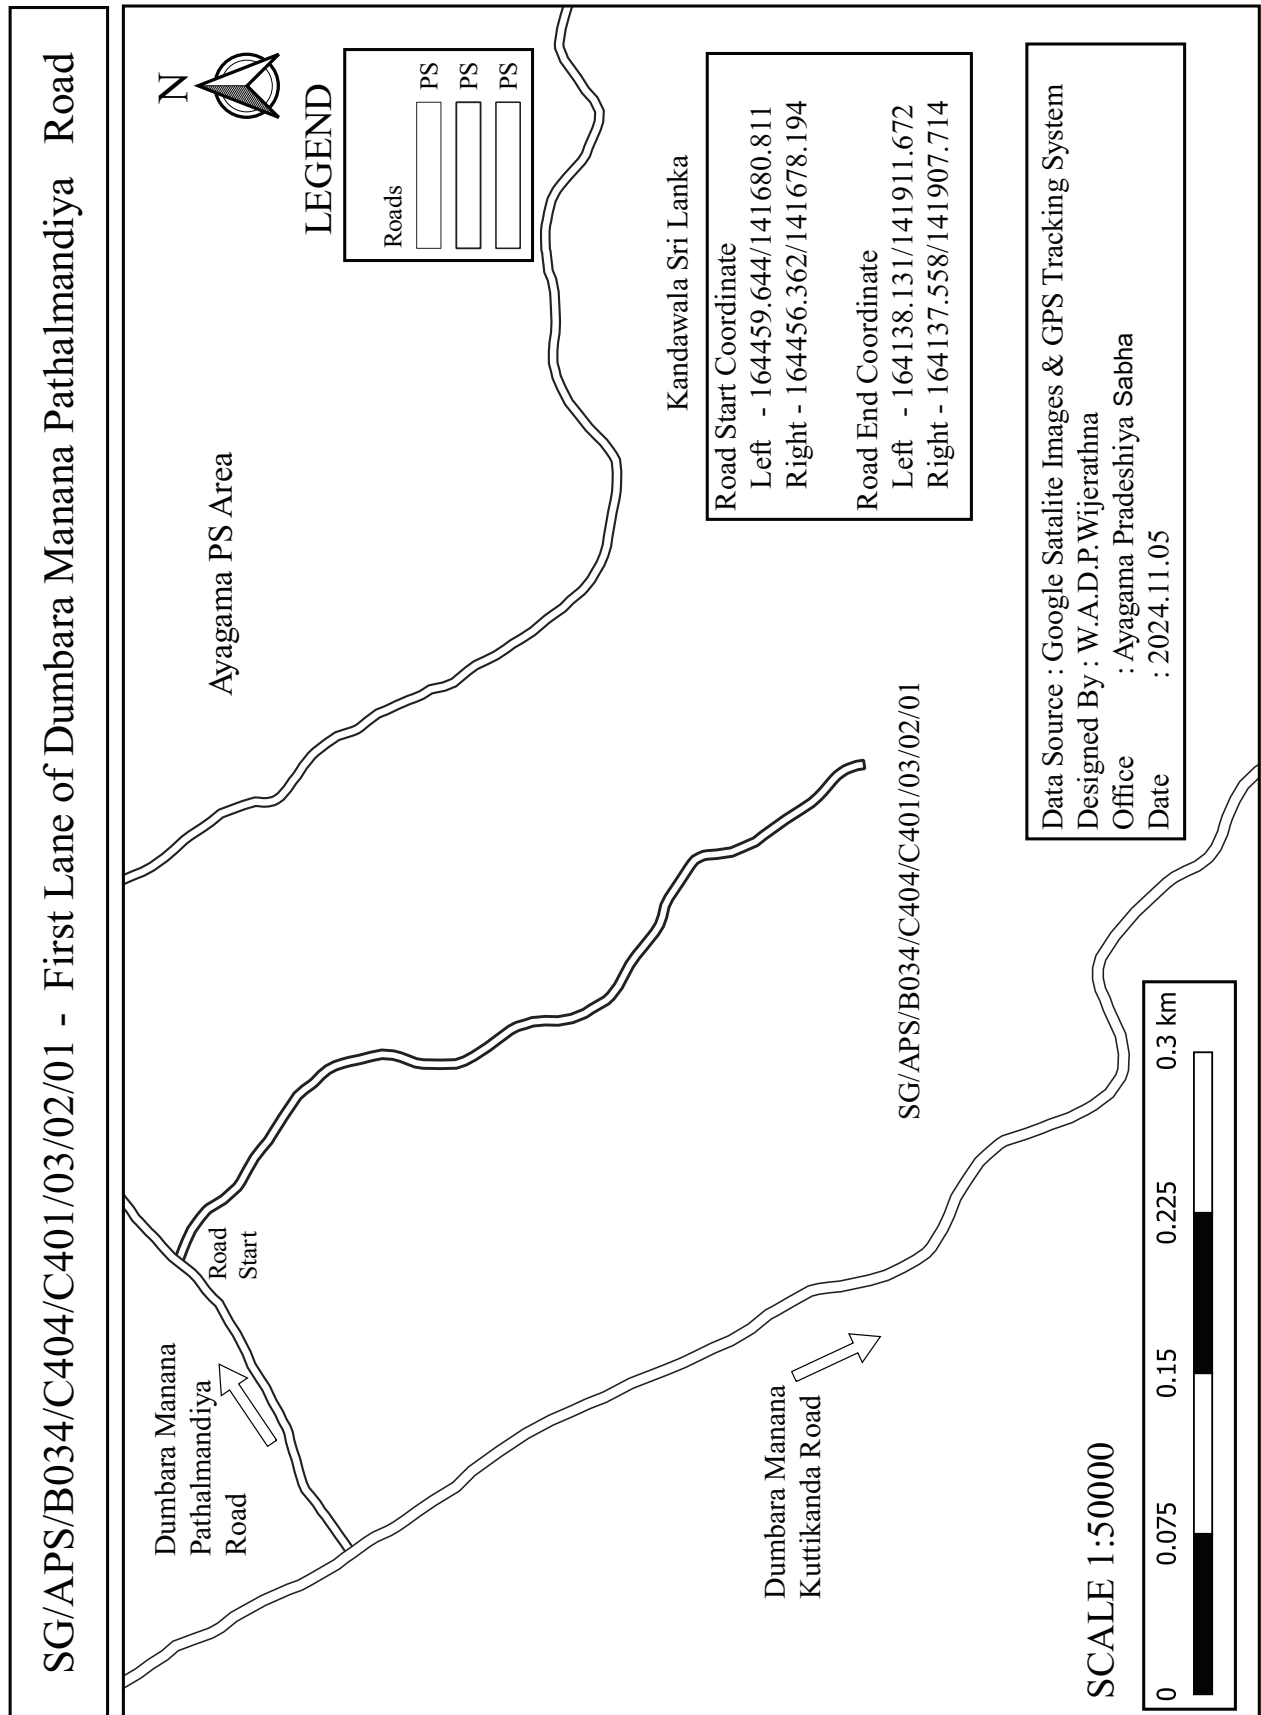


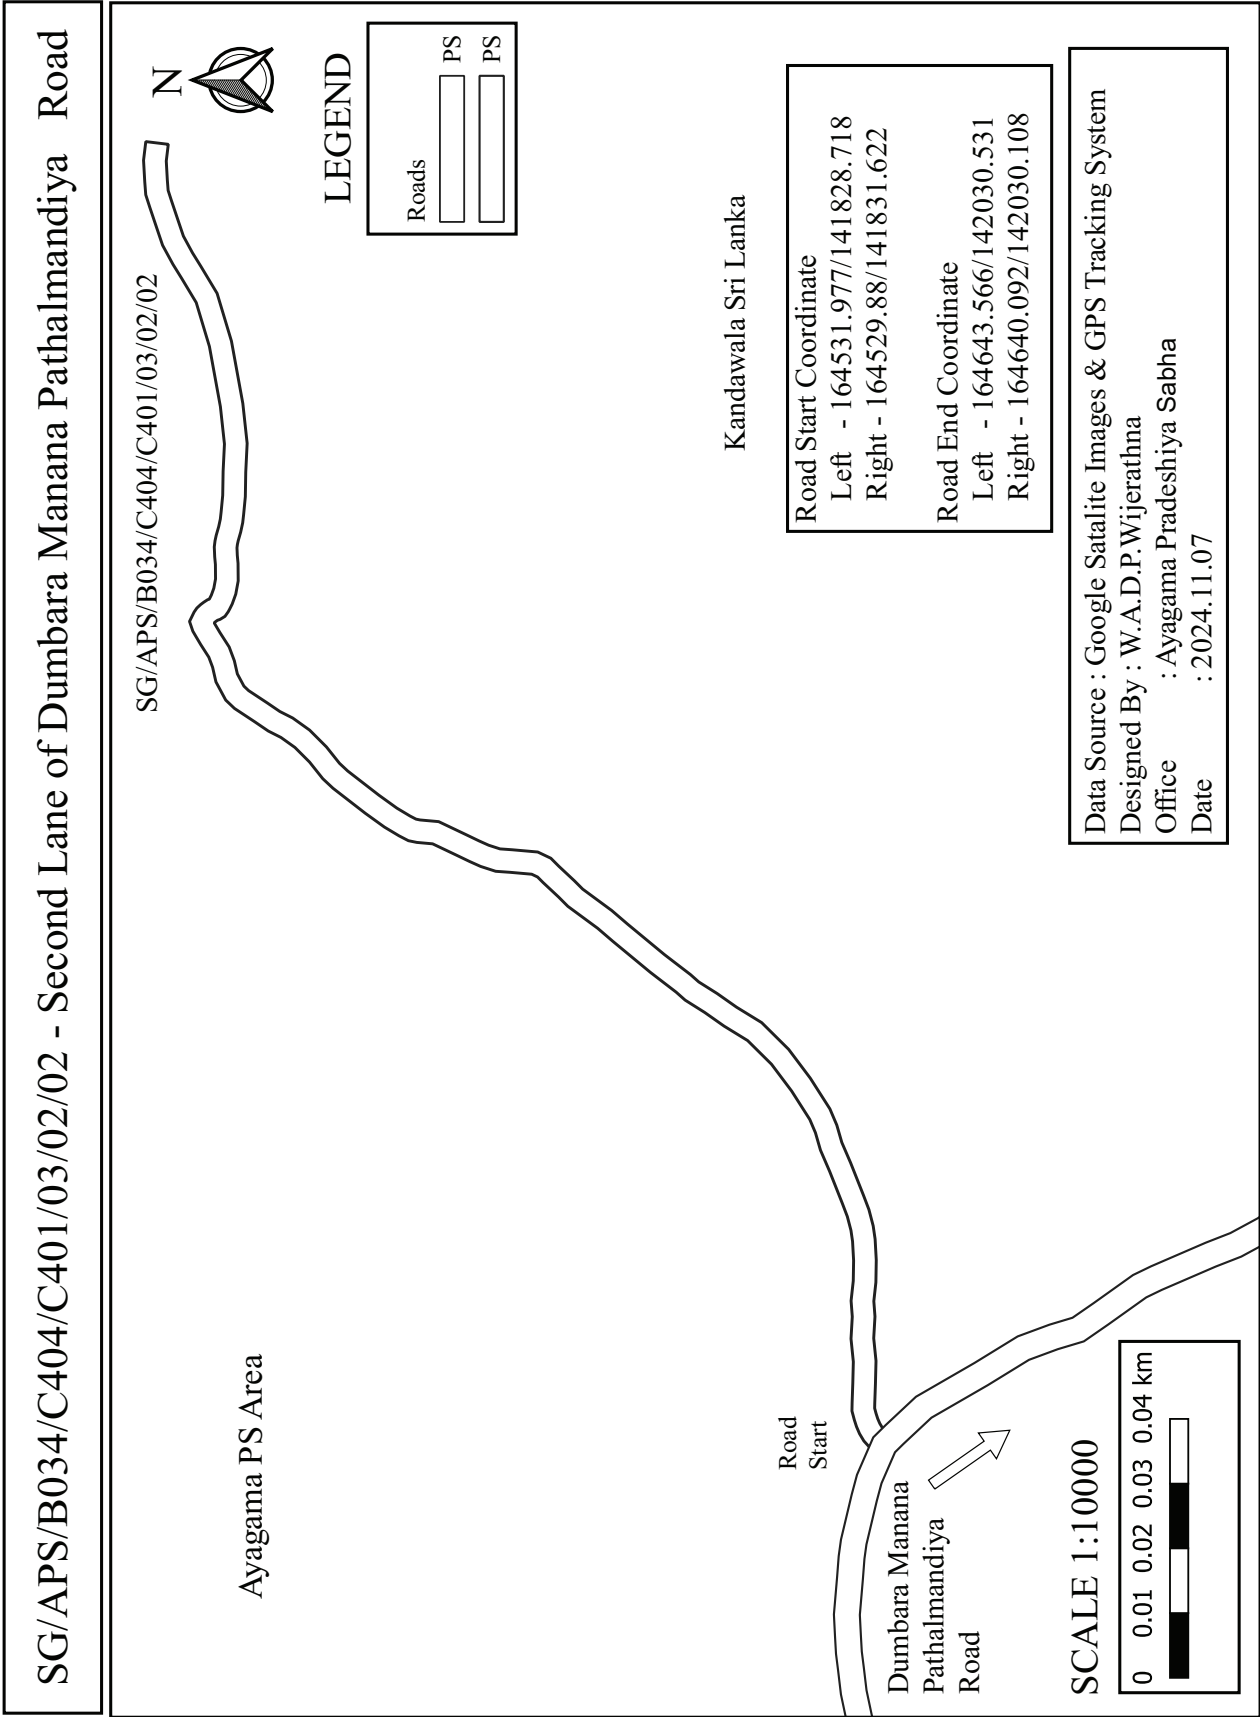


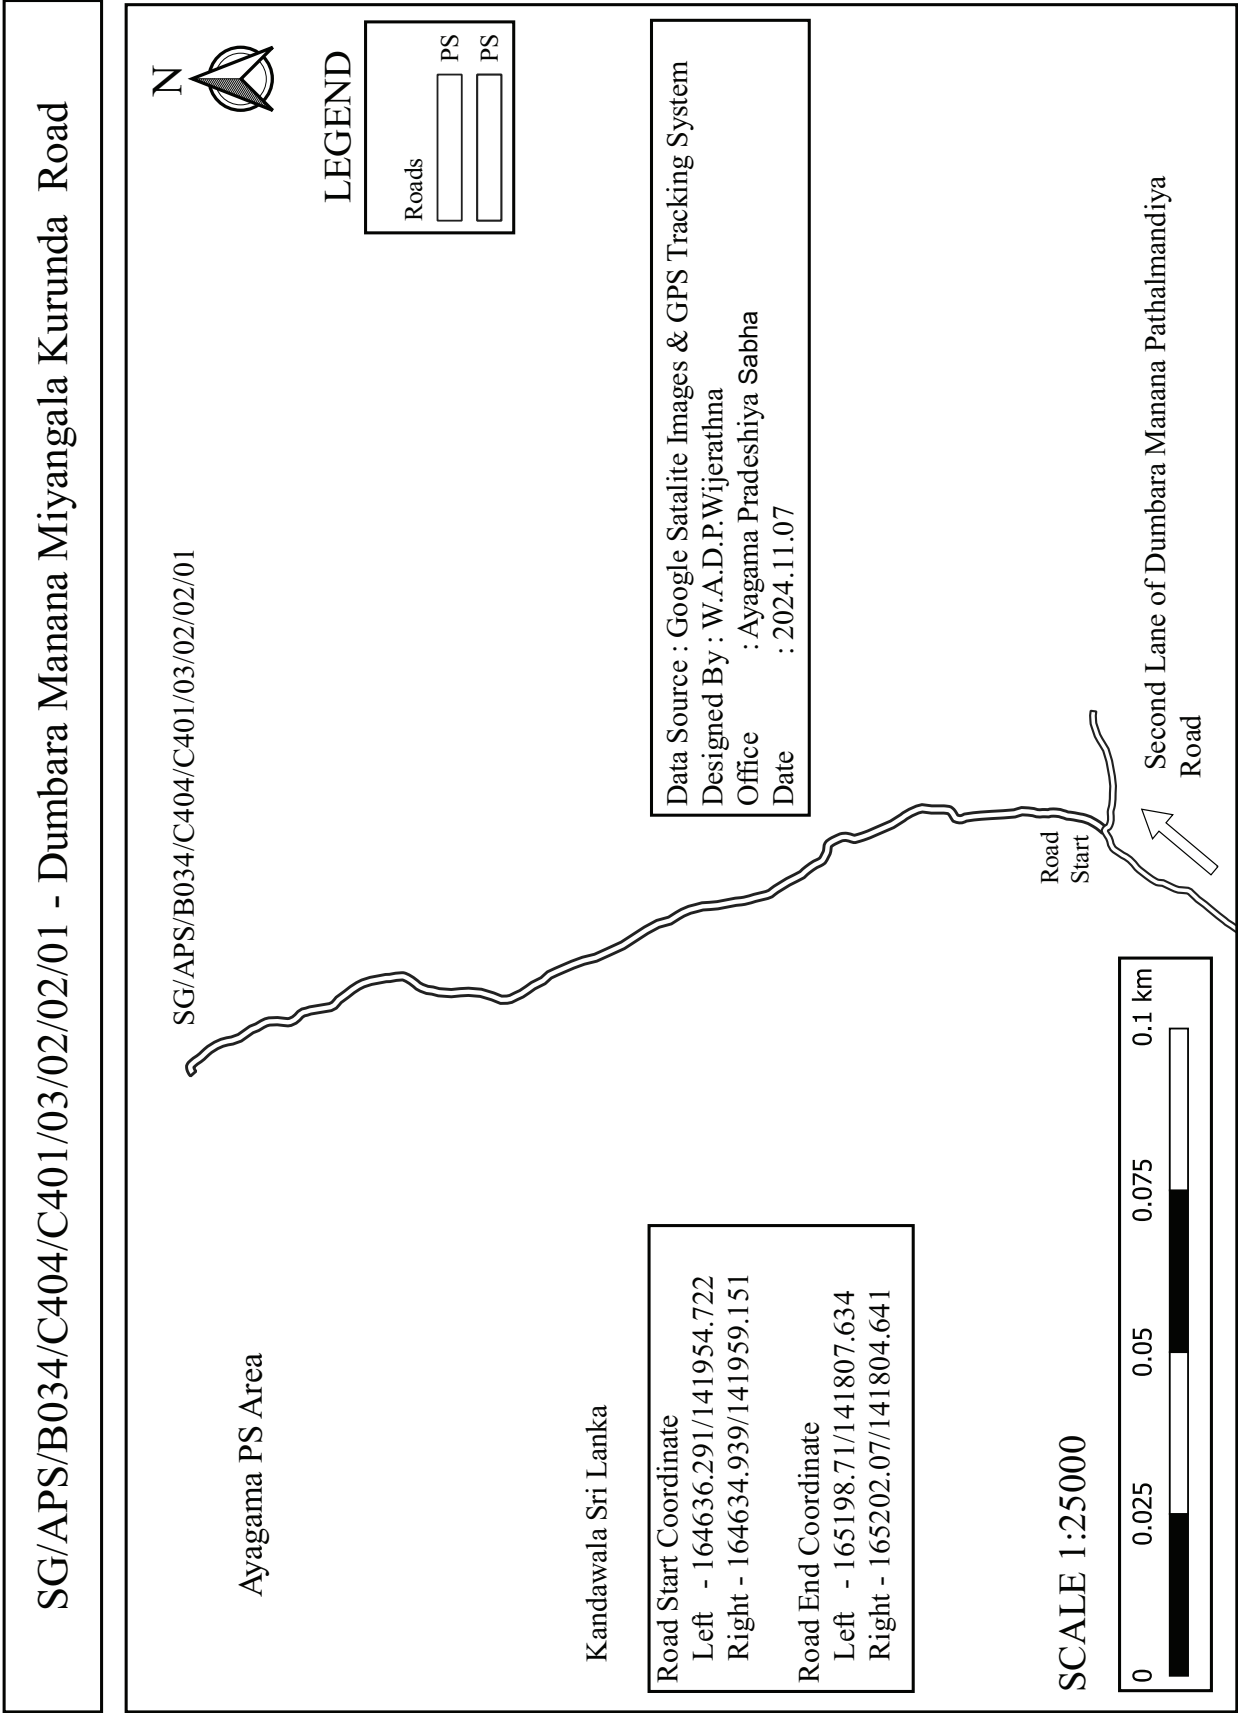




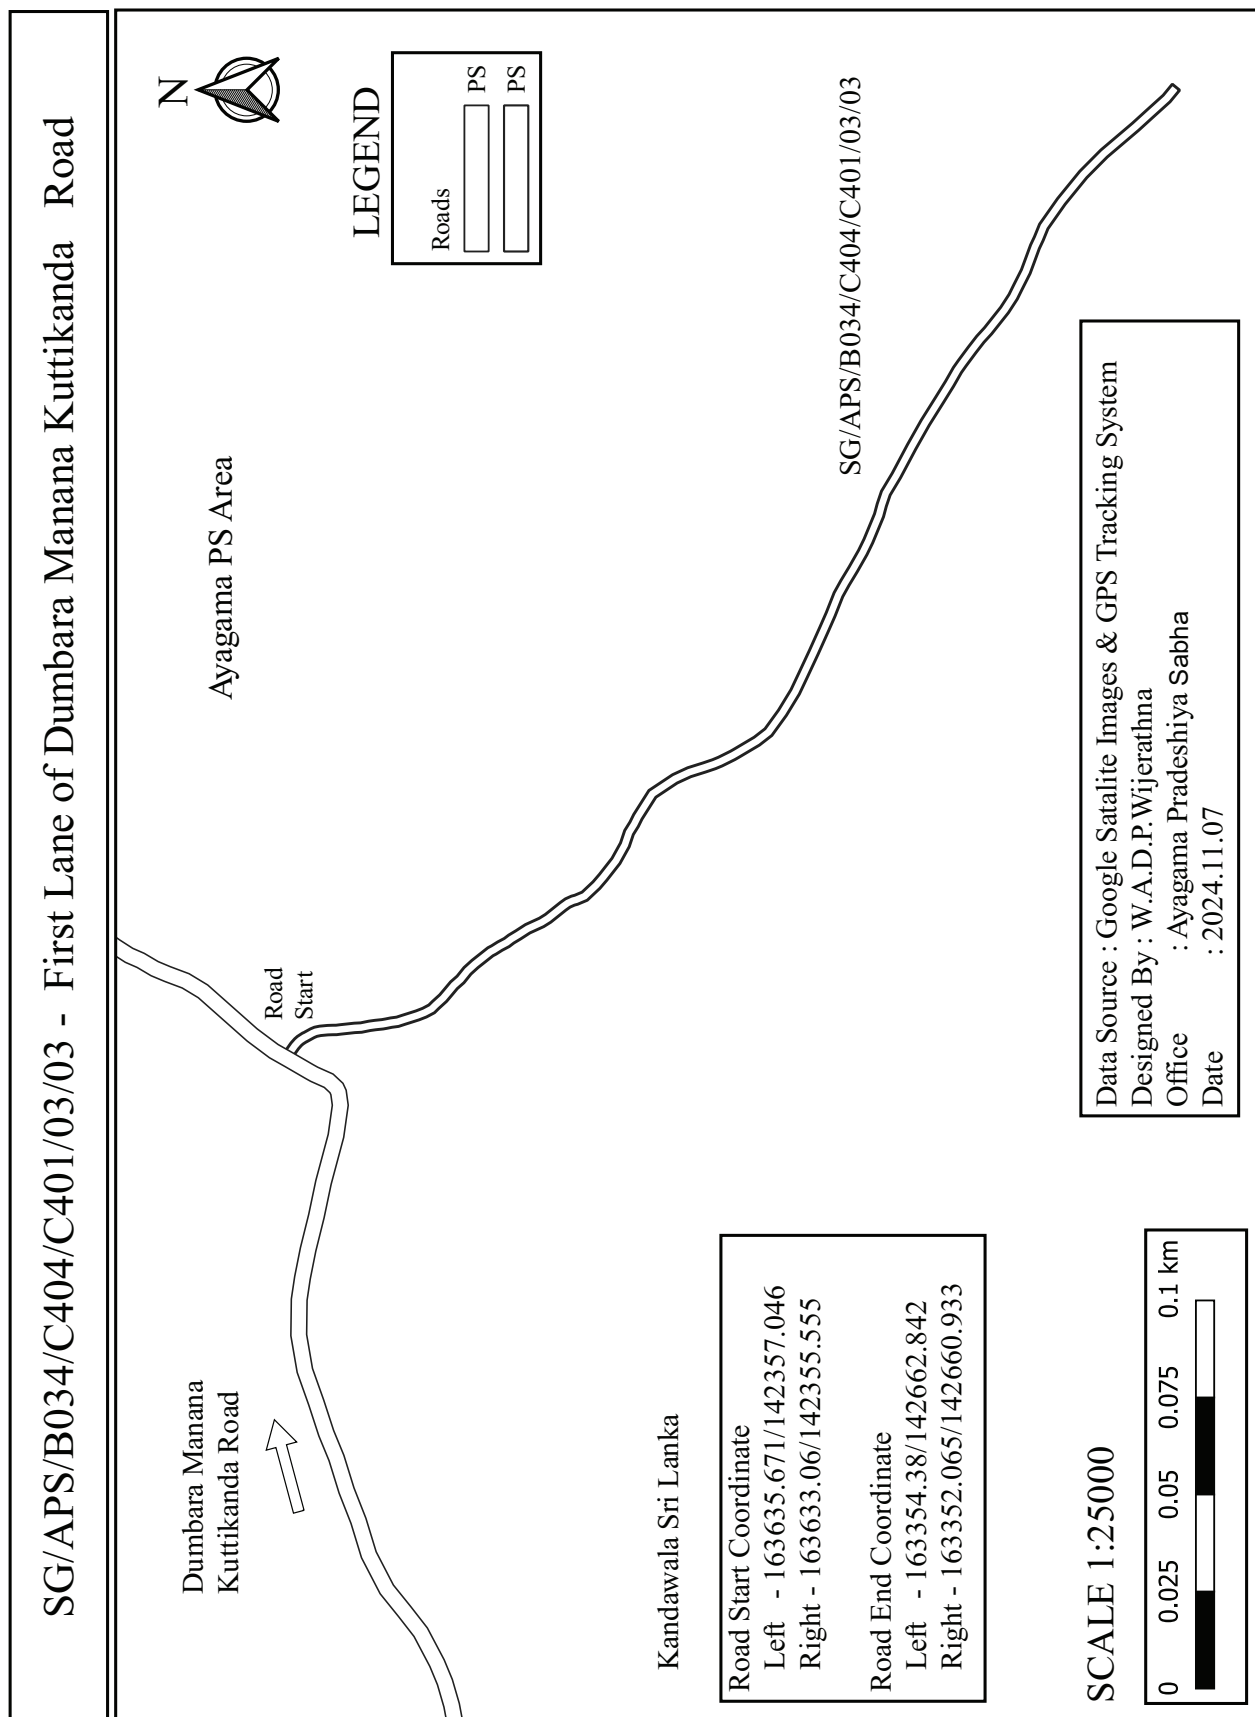


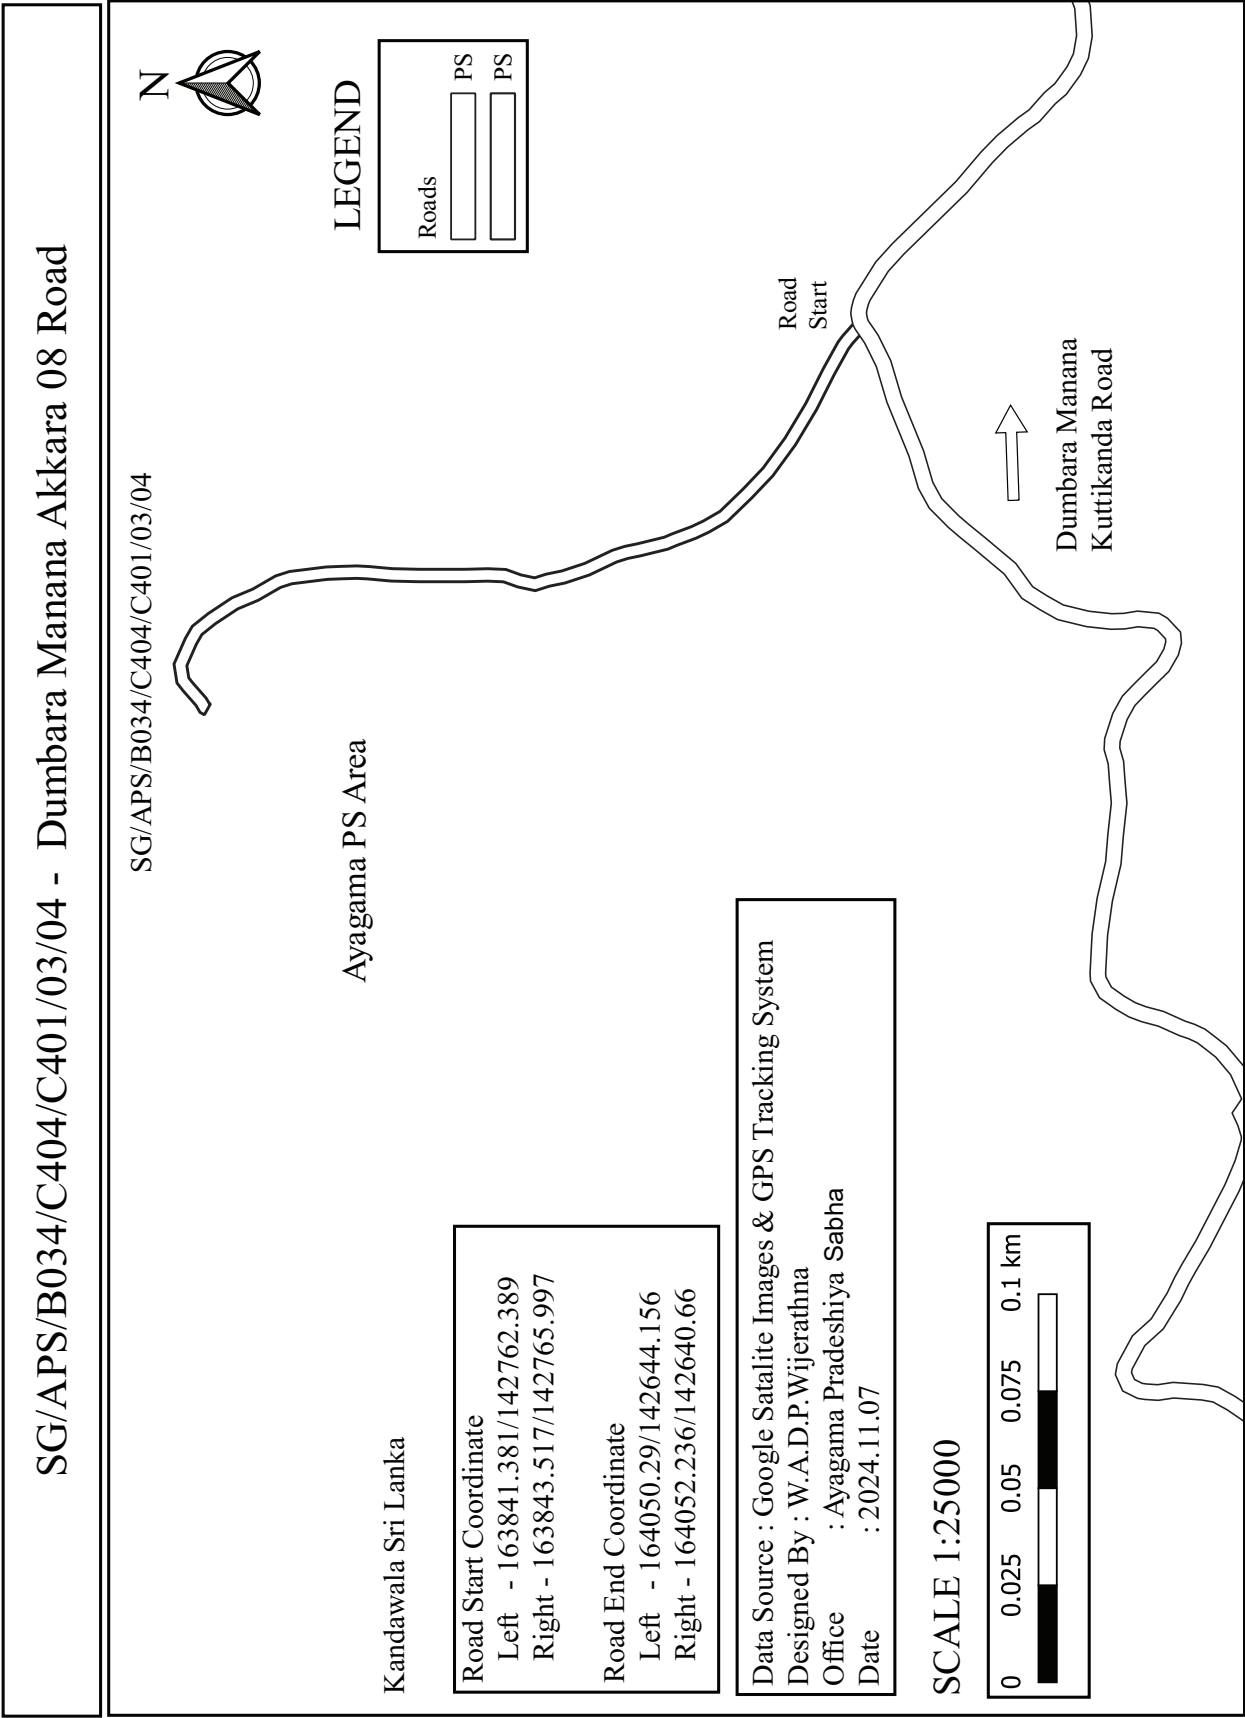


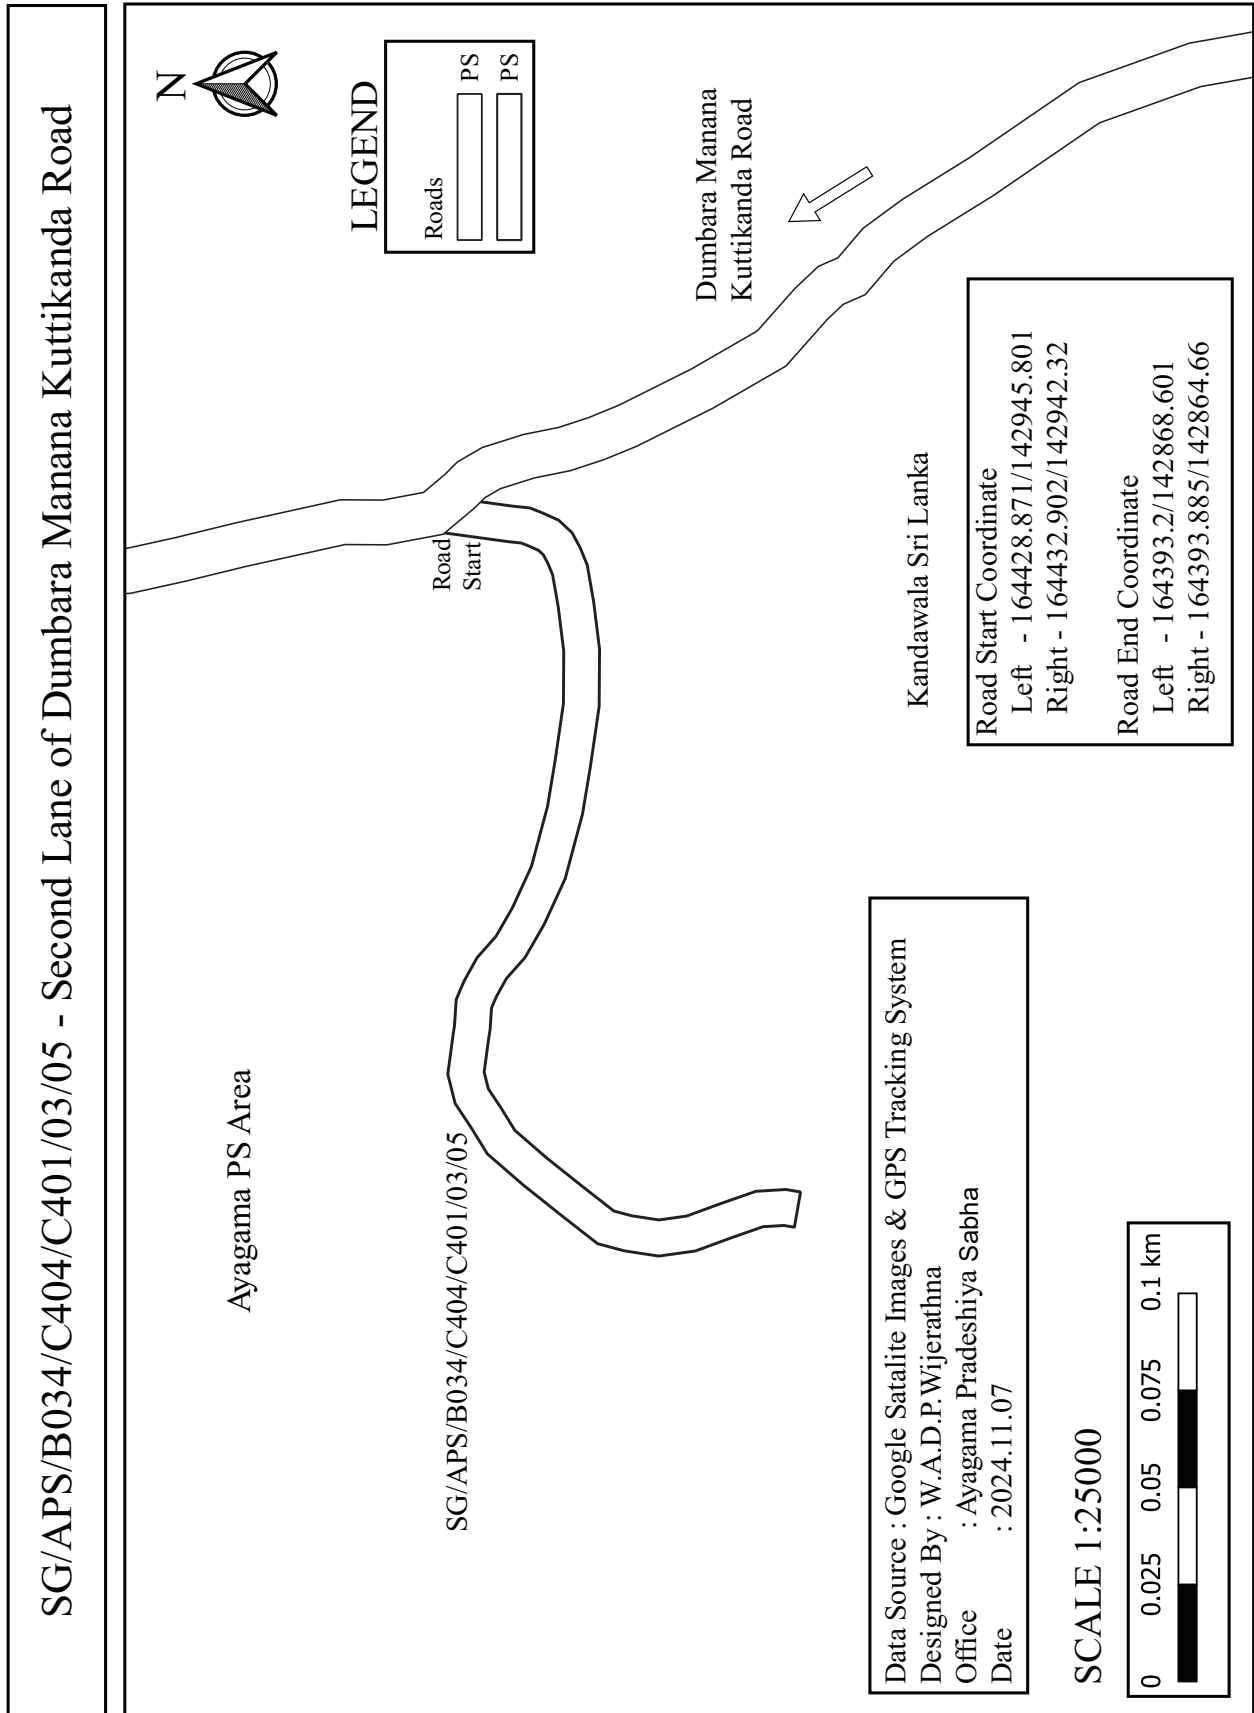

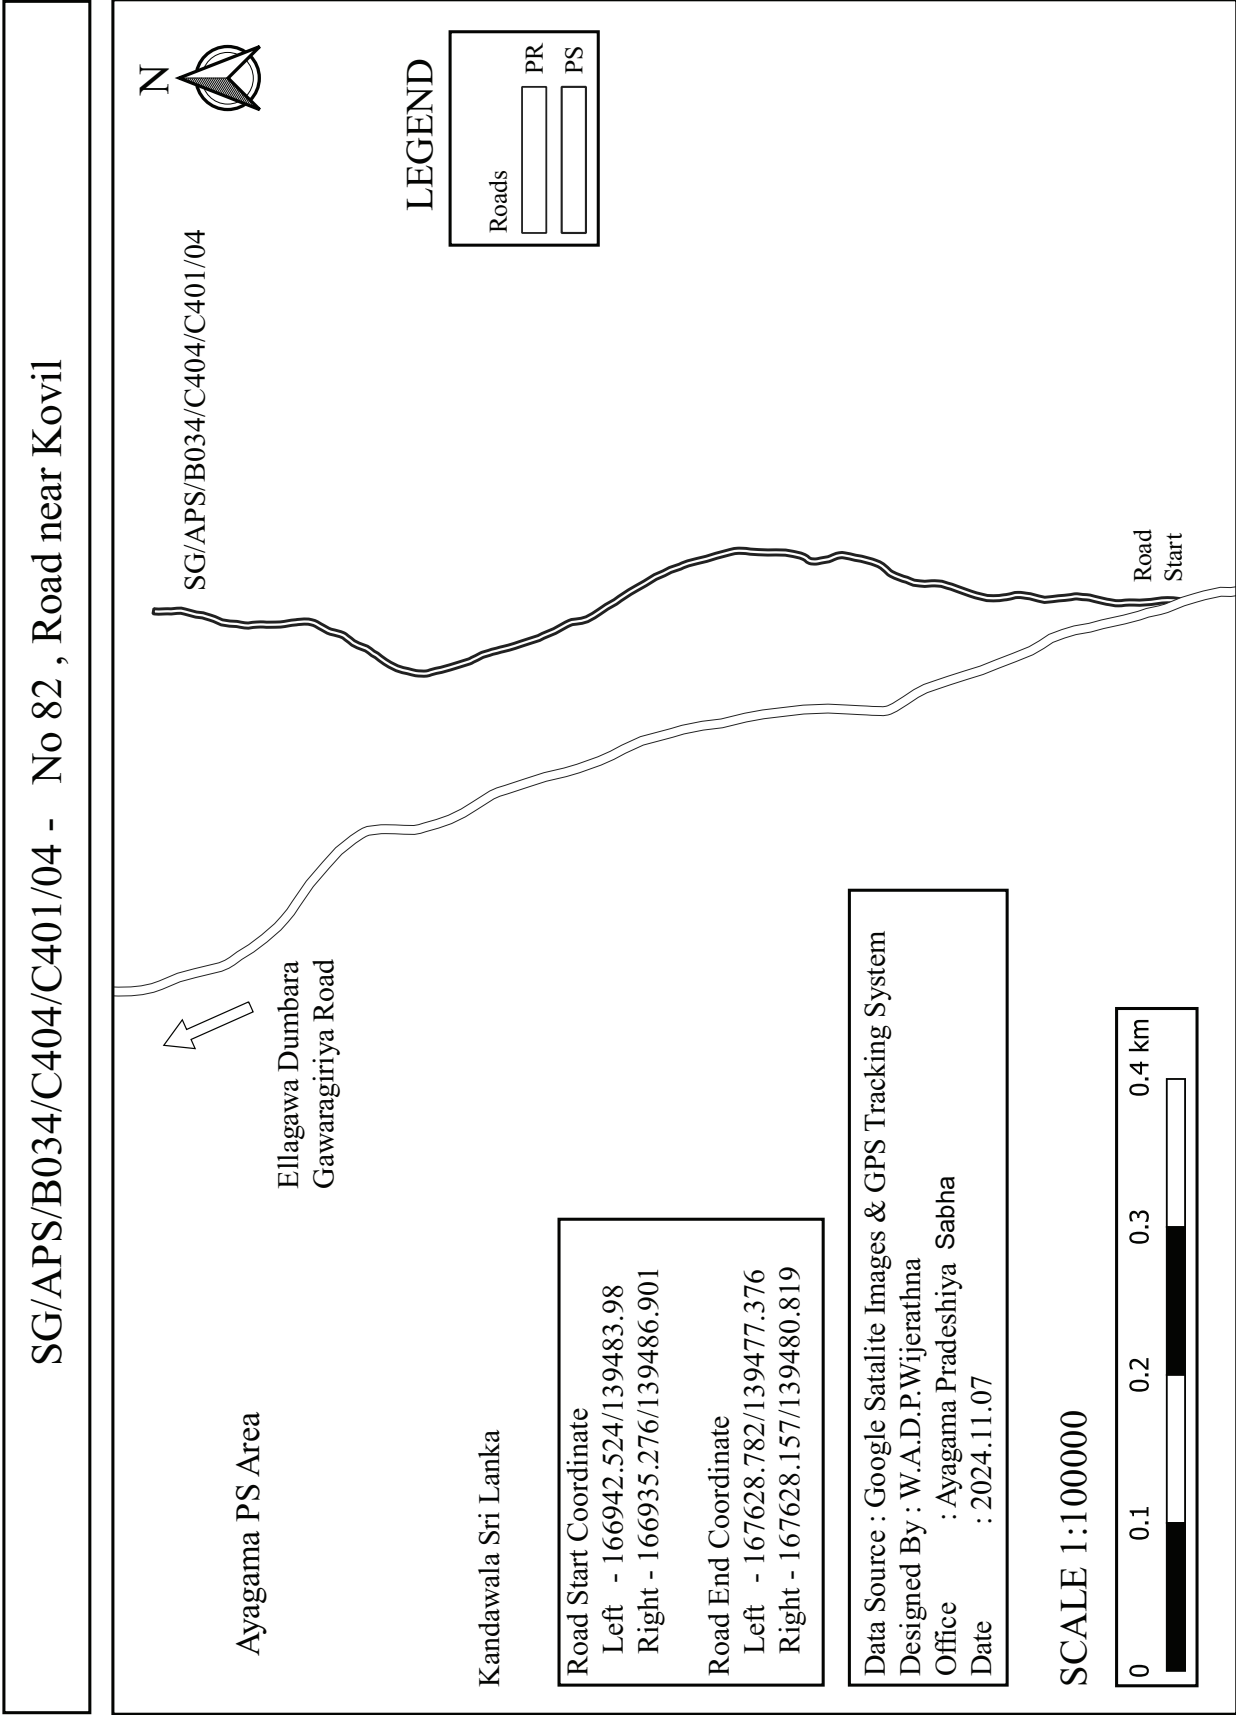



SG/APS/B034/C404/C401/05 - Footpath No.82 Dumbara

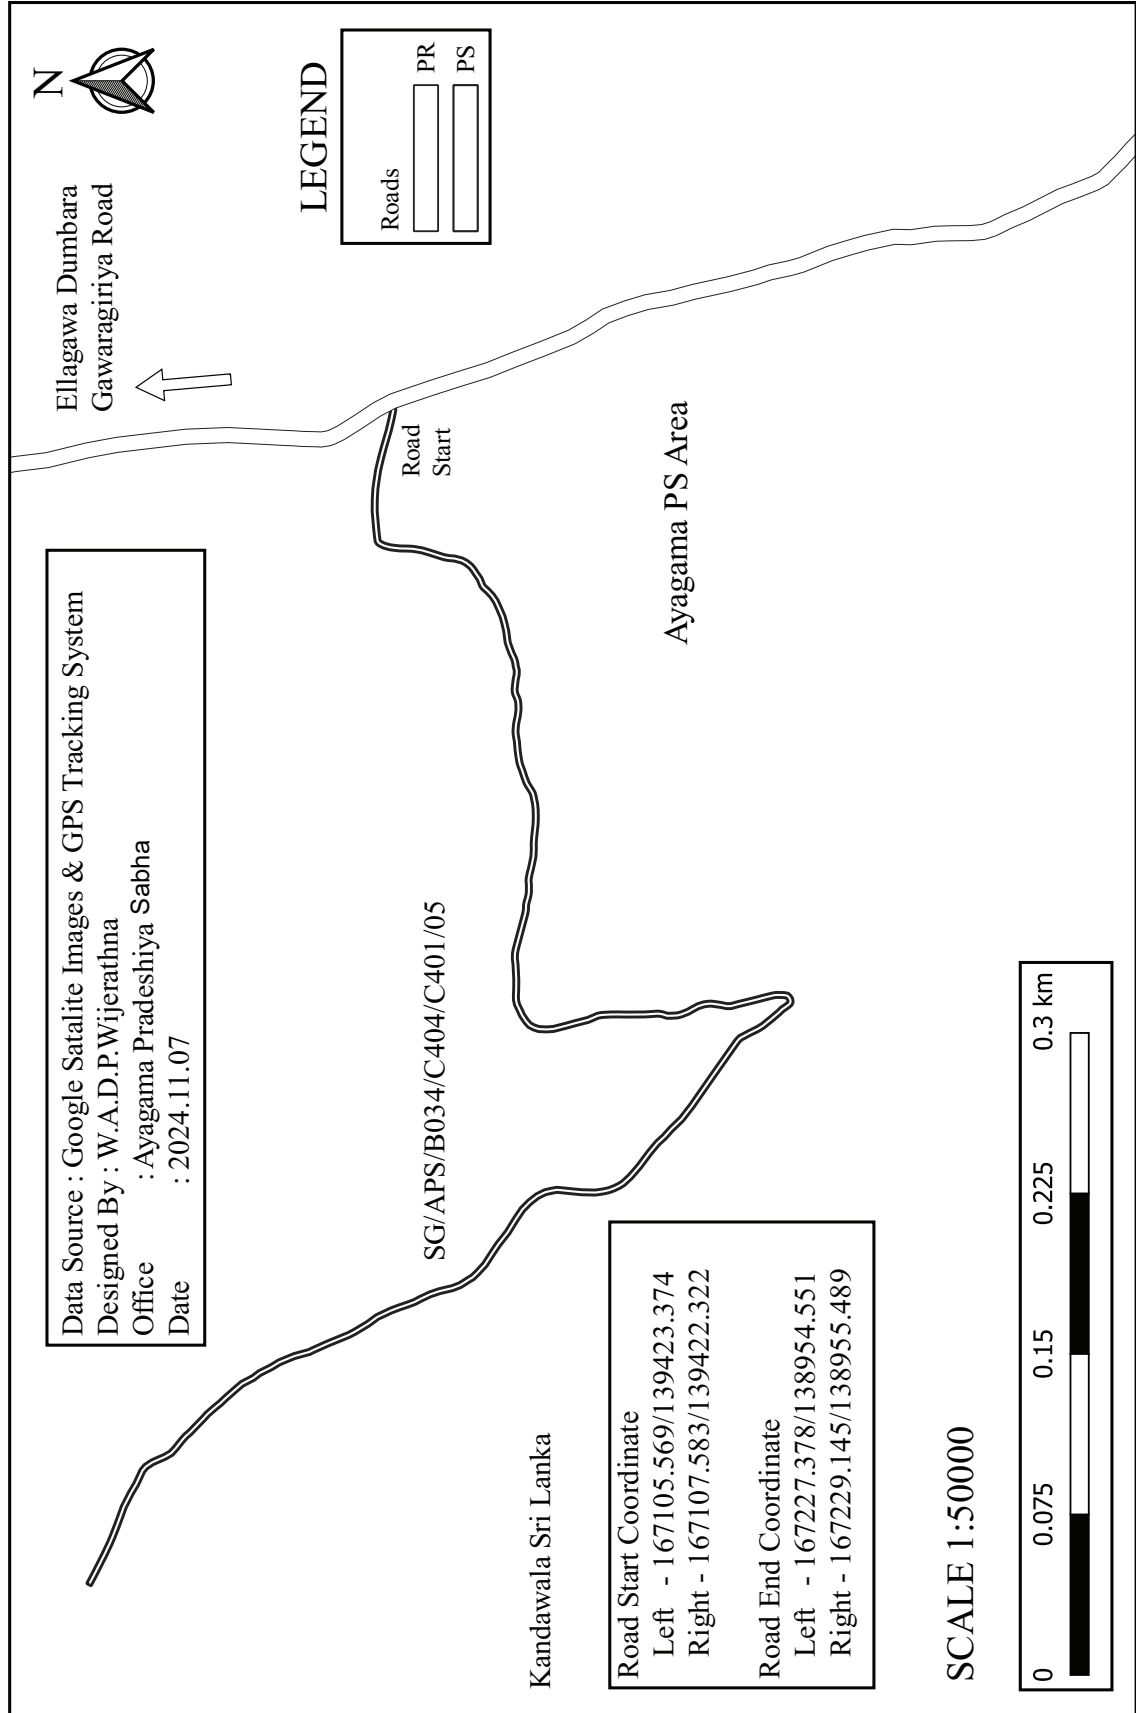

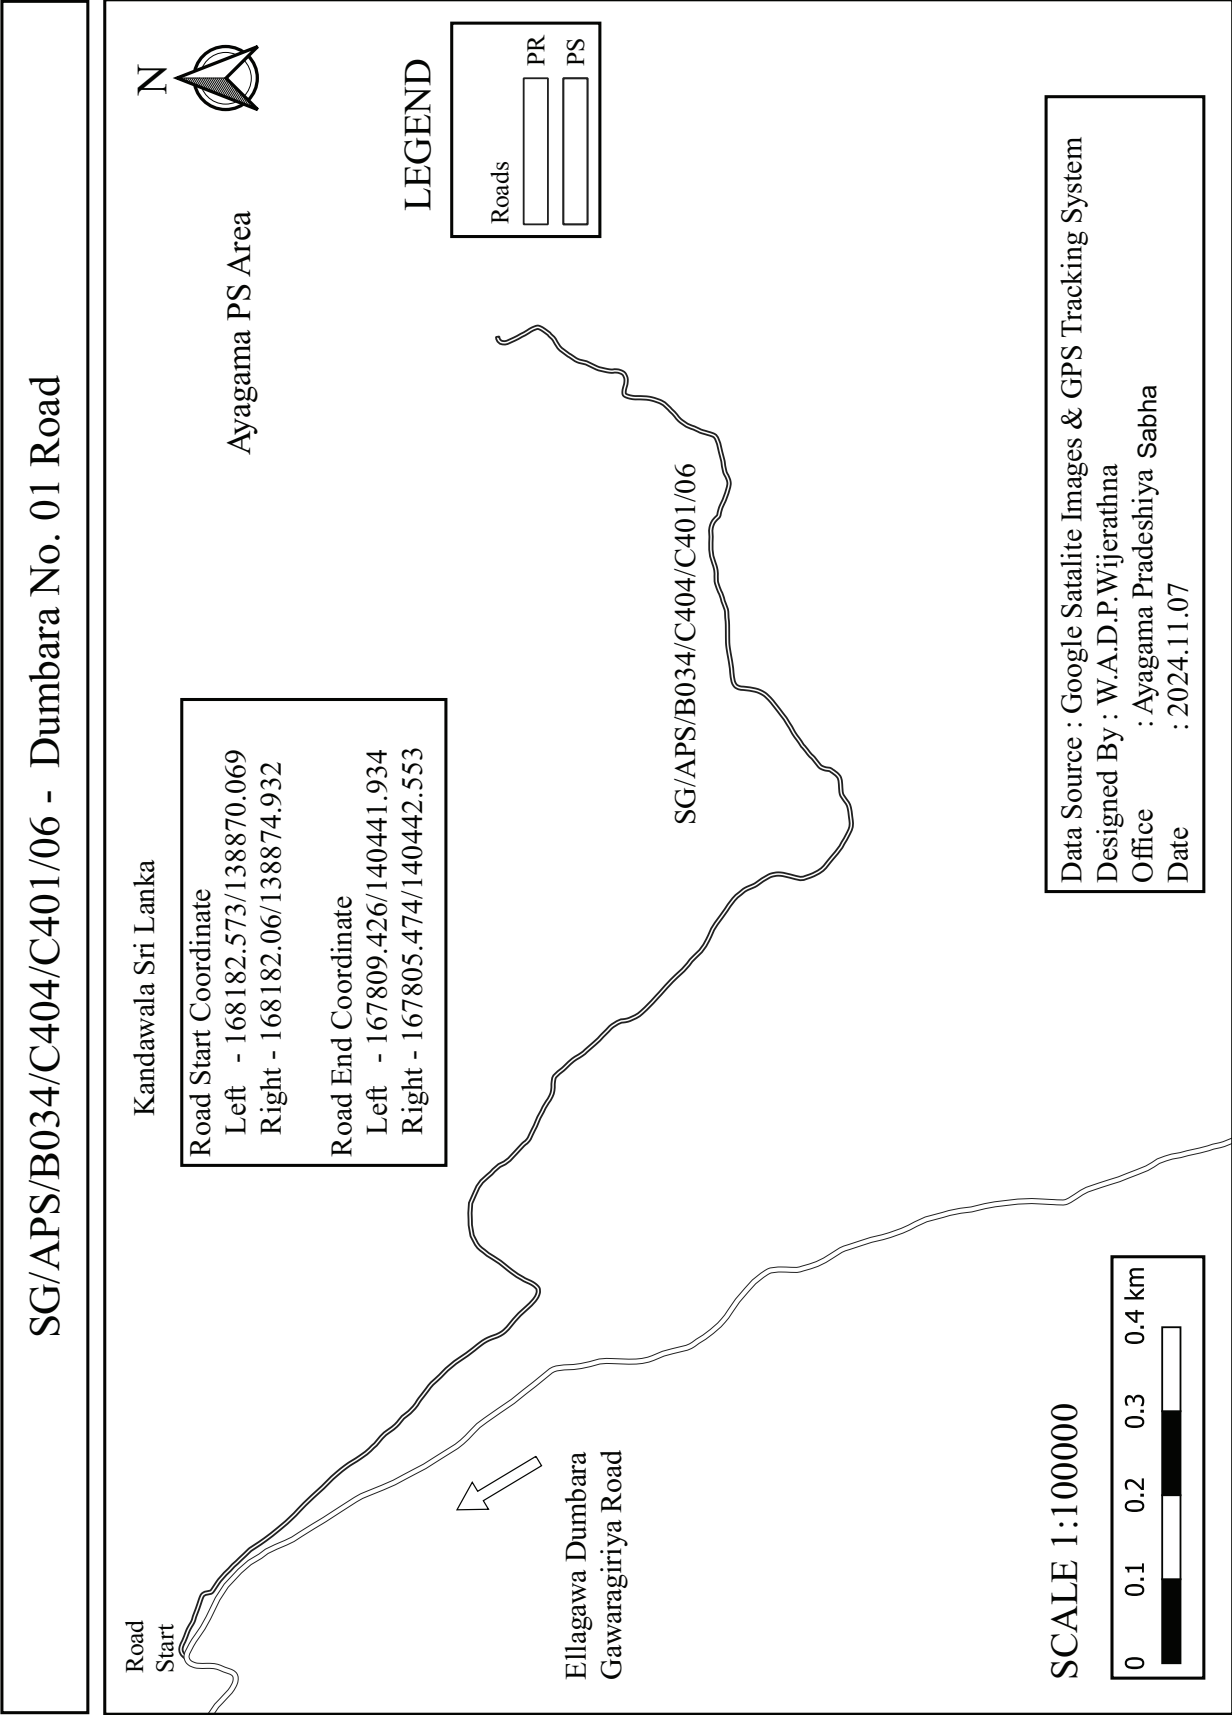



SG/APS/B034/C404/C401/07 - Dumbara Medikella Ihala Road

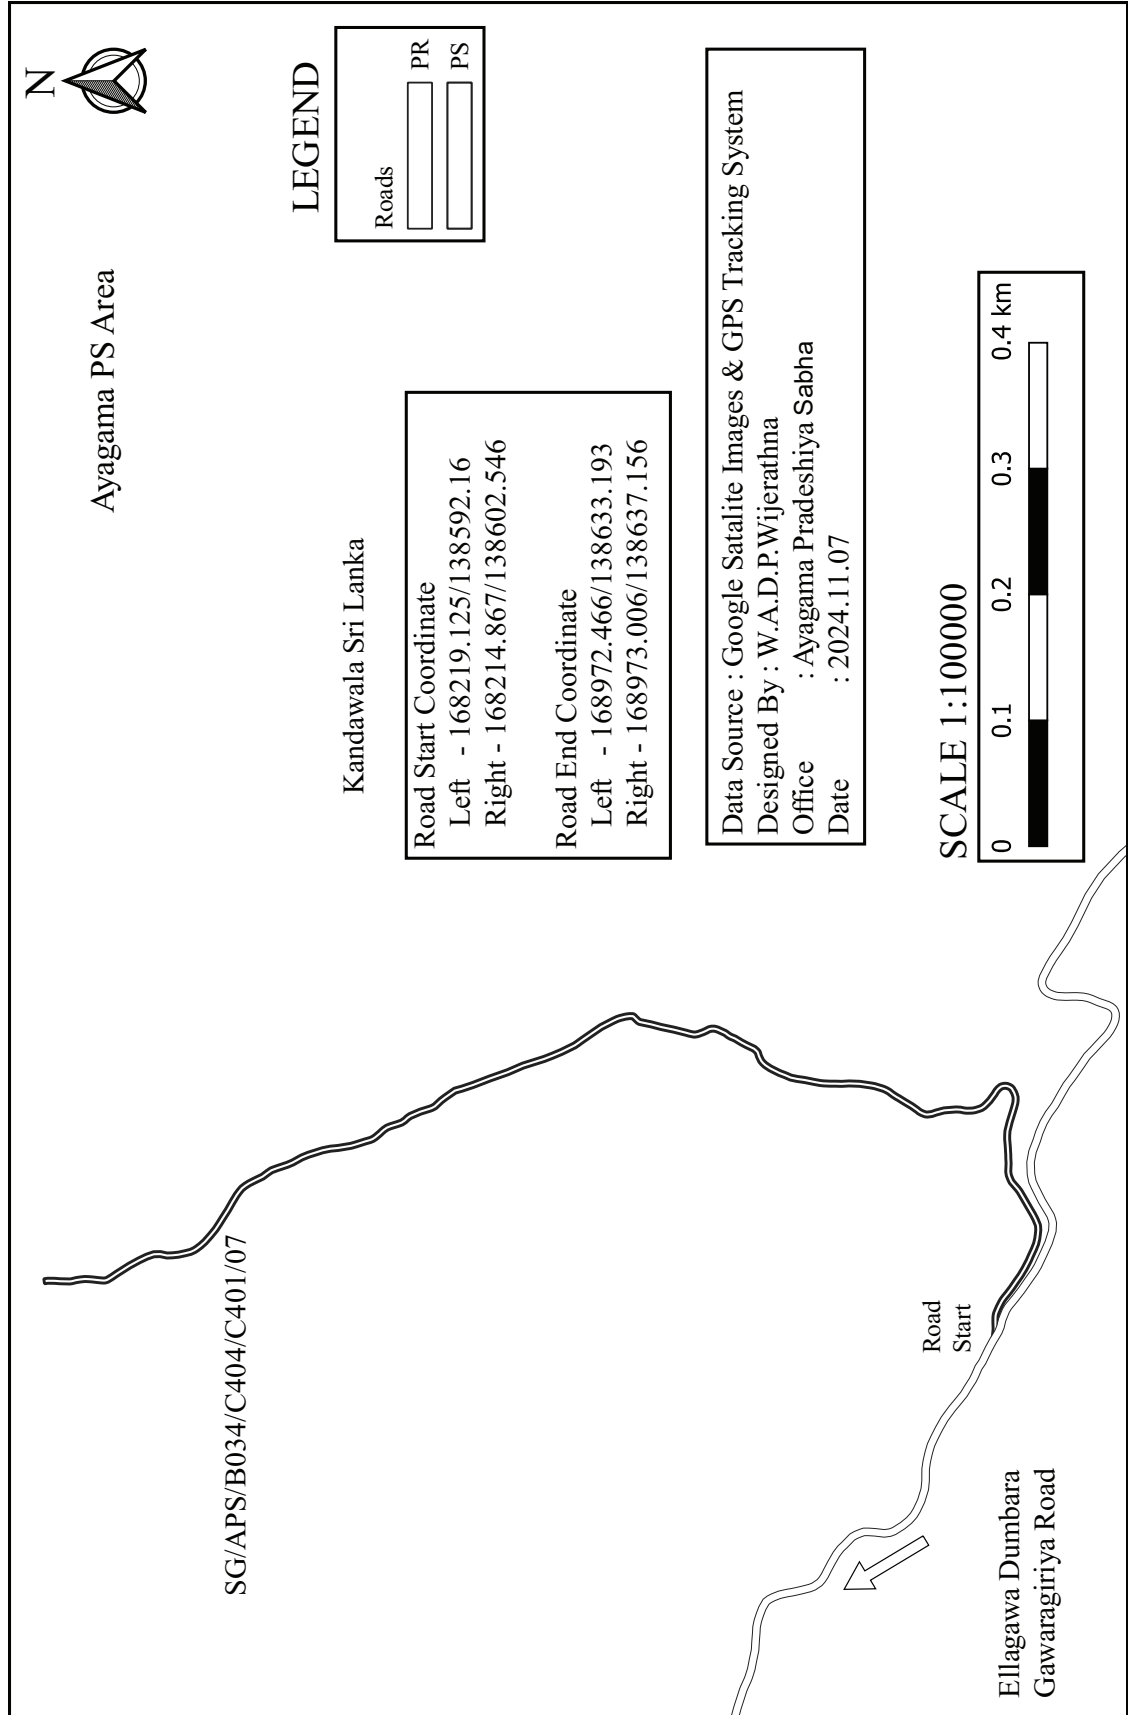


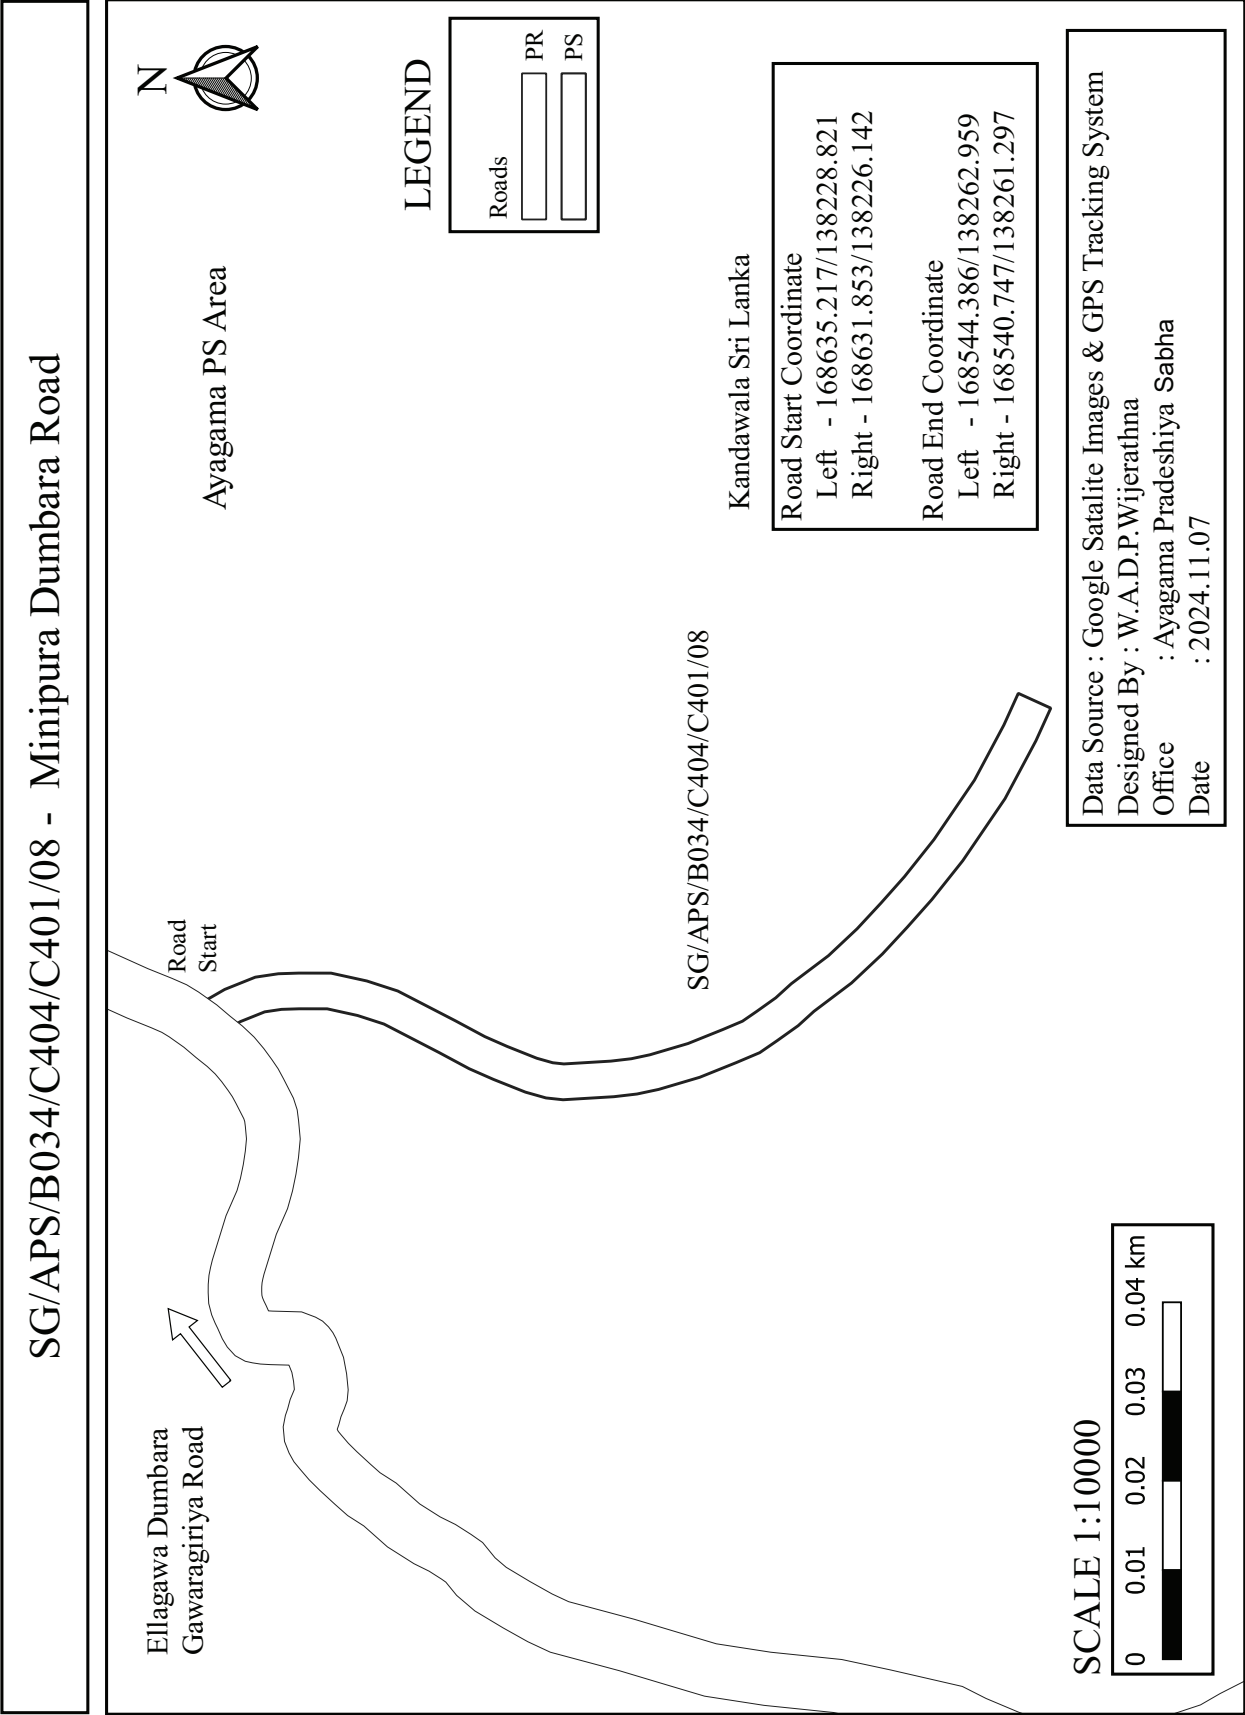



SG/APS/B034/C404/C401/09 - Minipura Dumbara Ataheraliyagoda Road

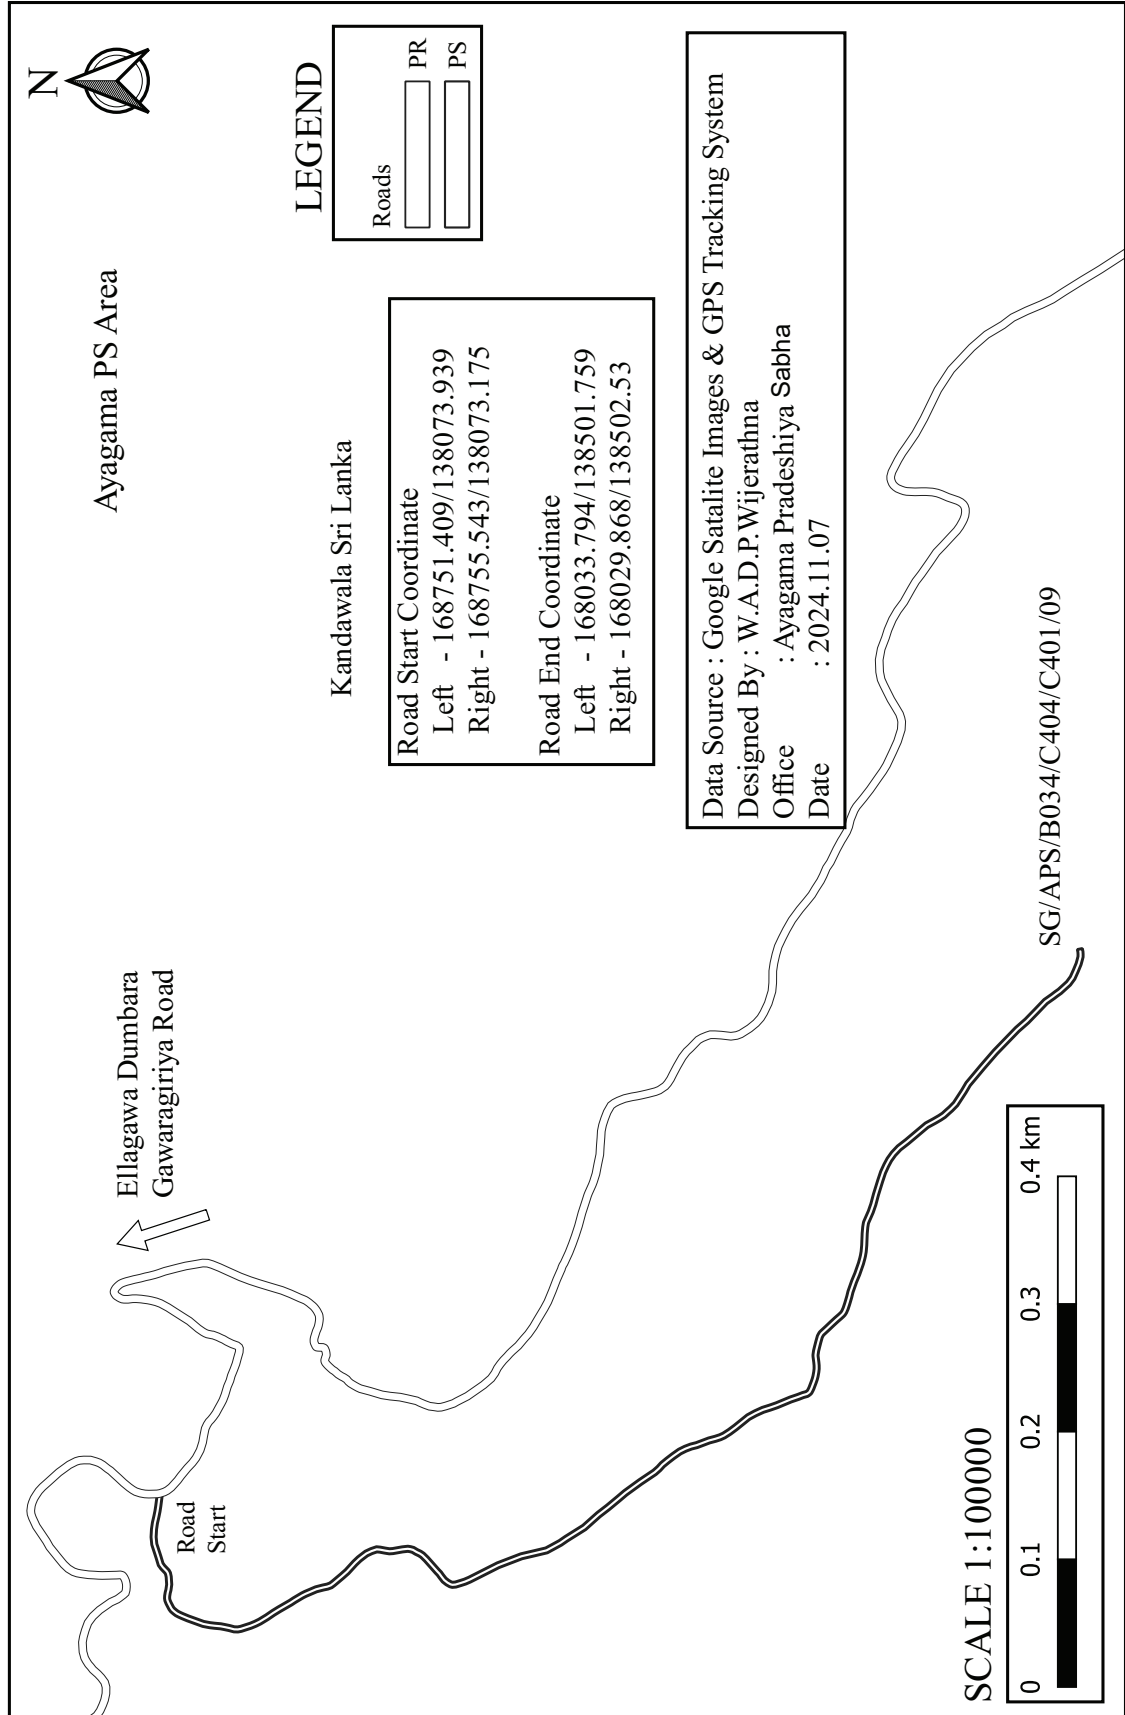


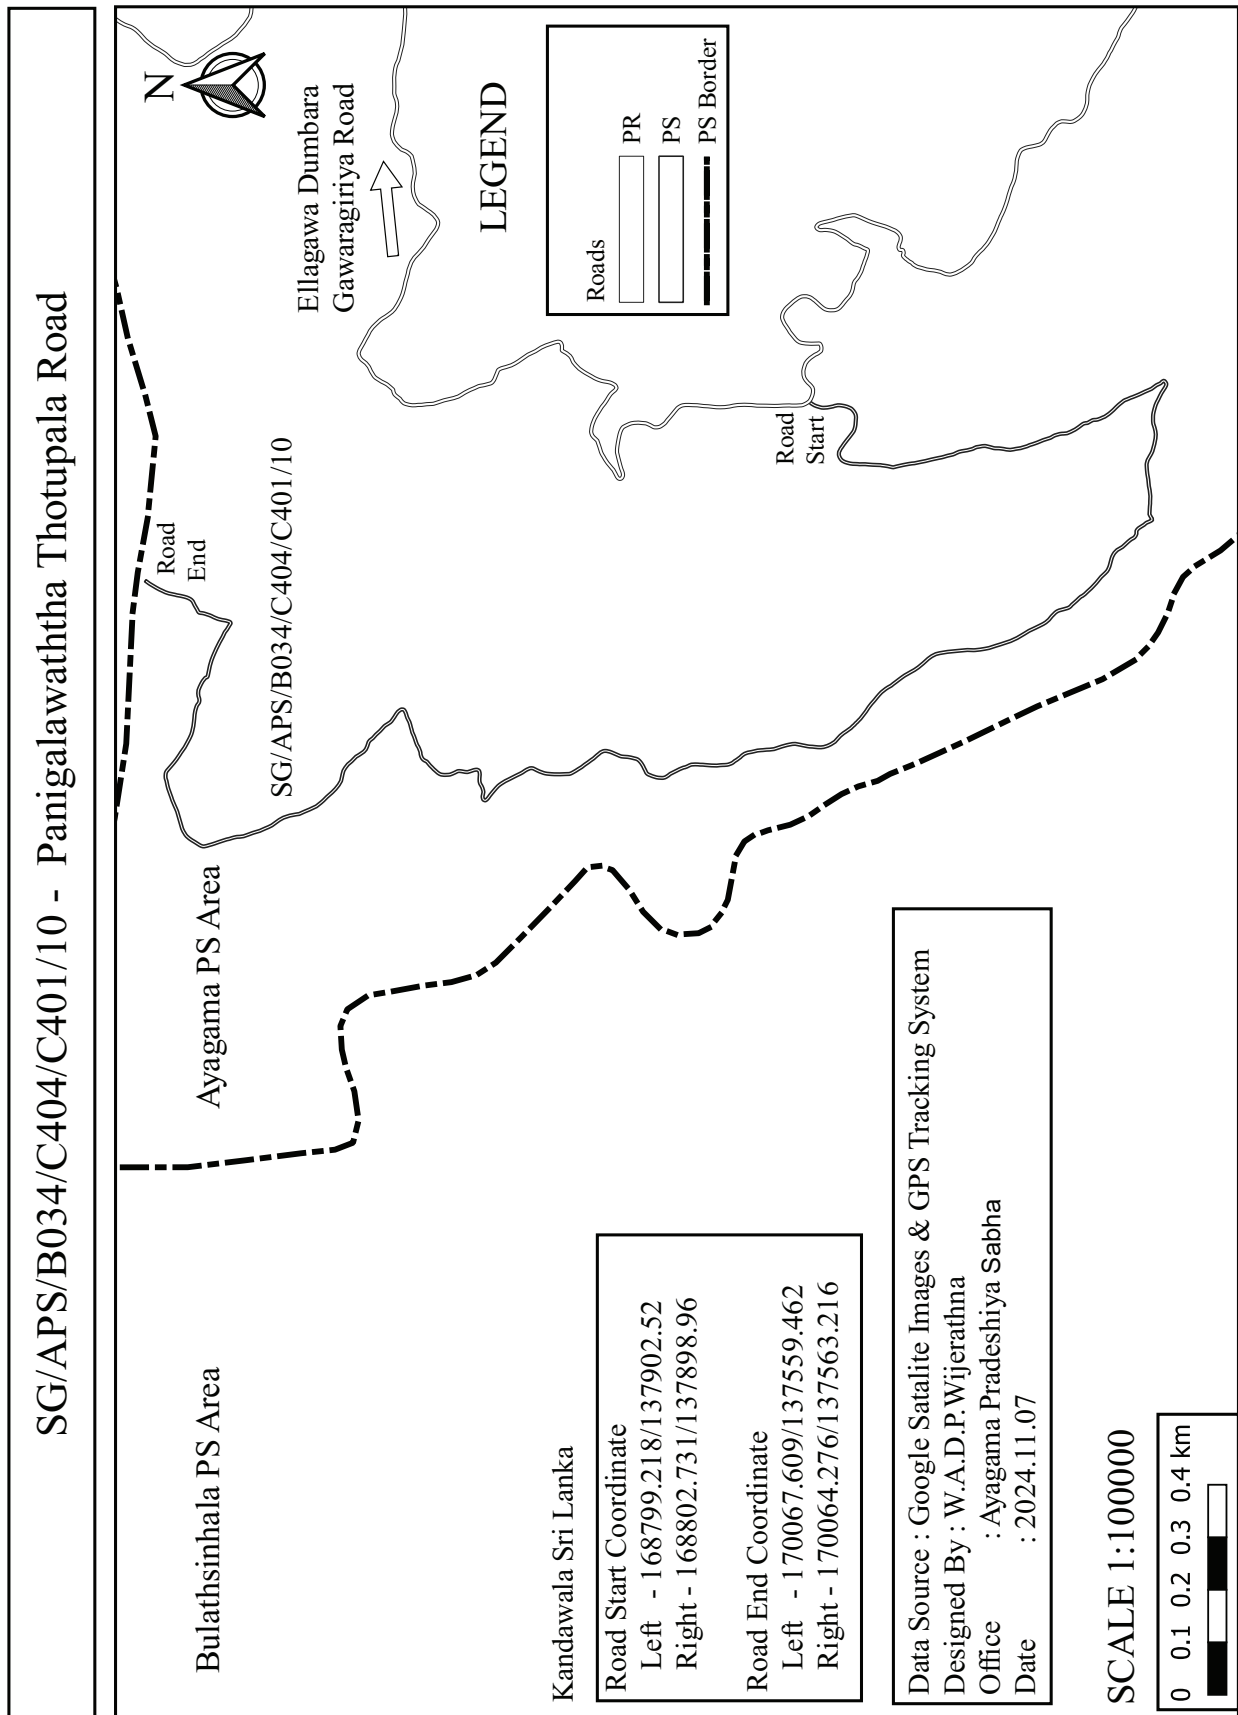


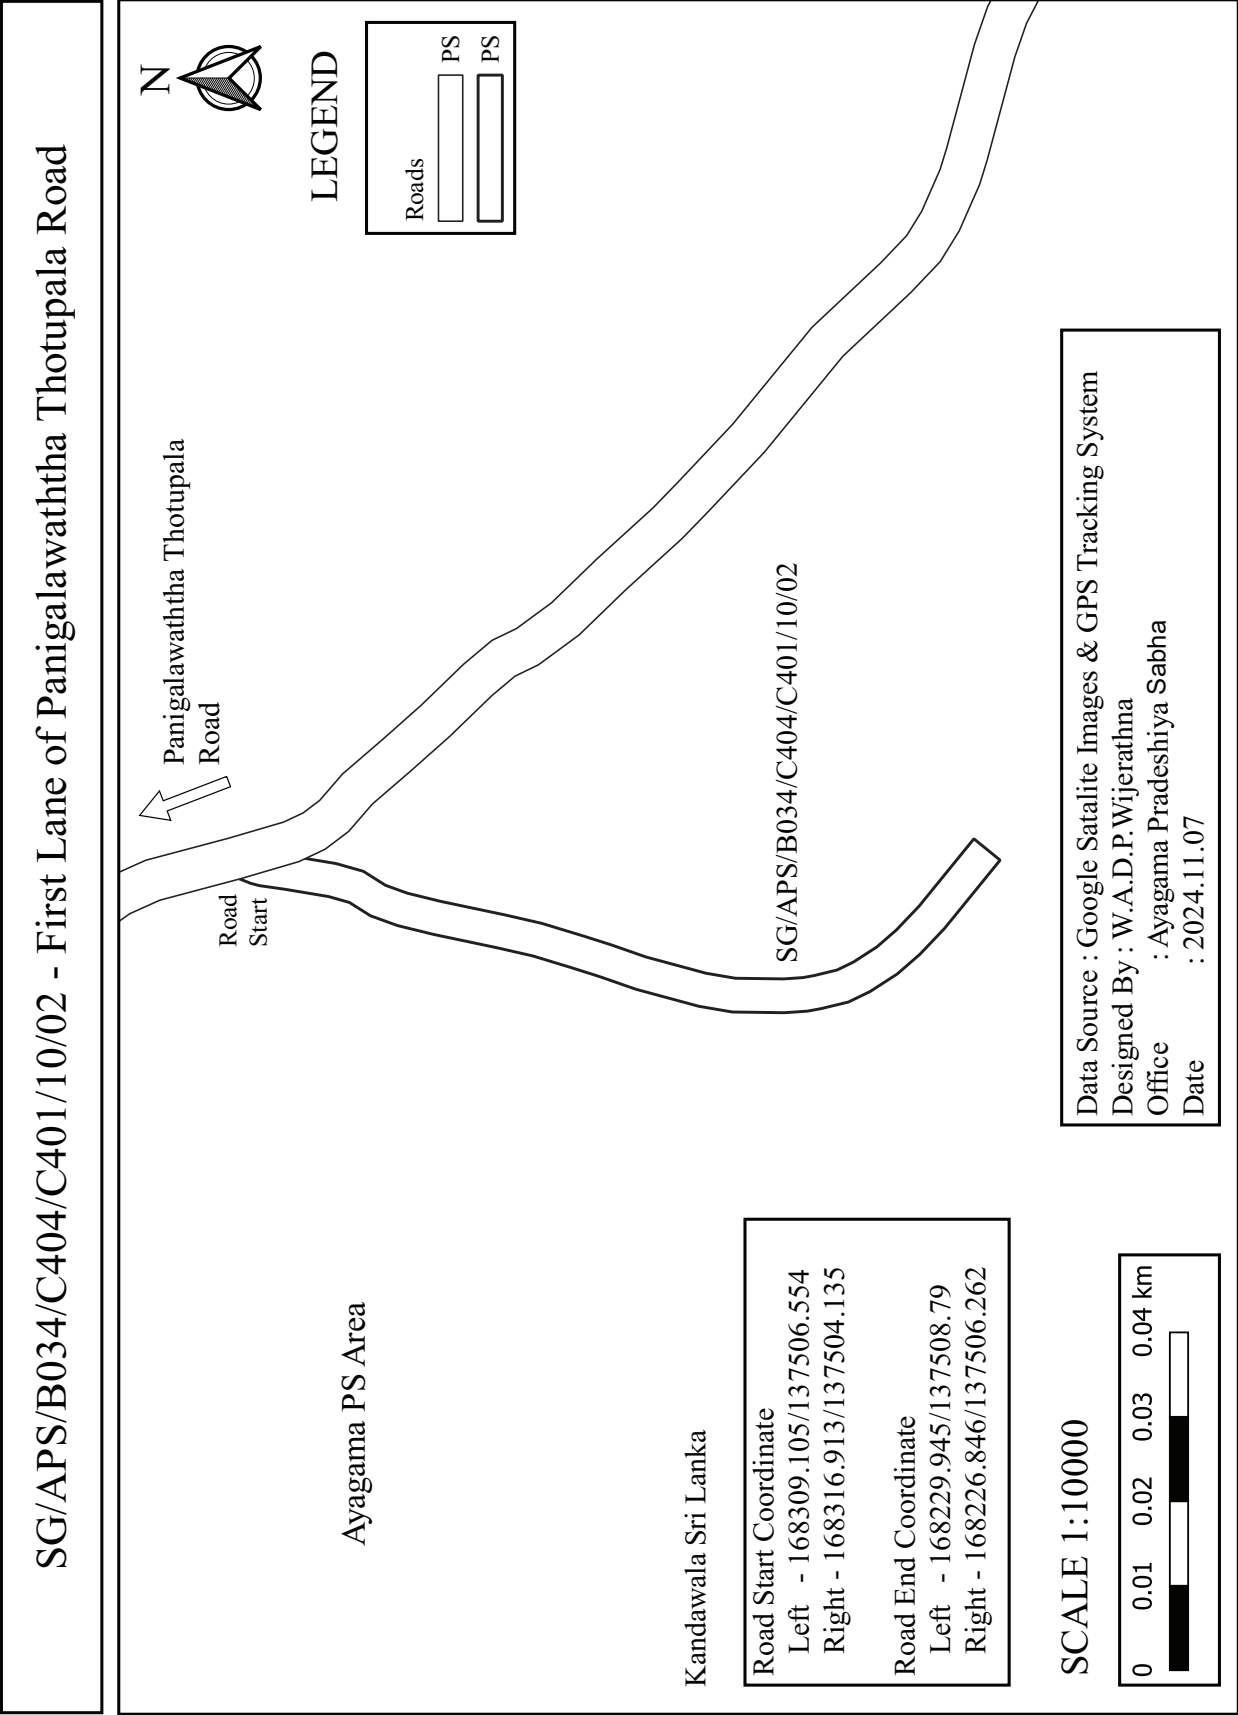


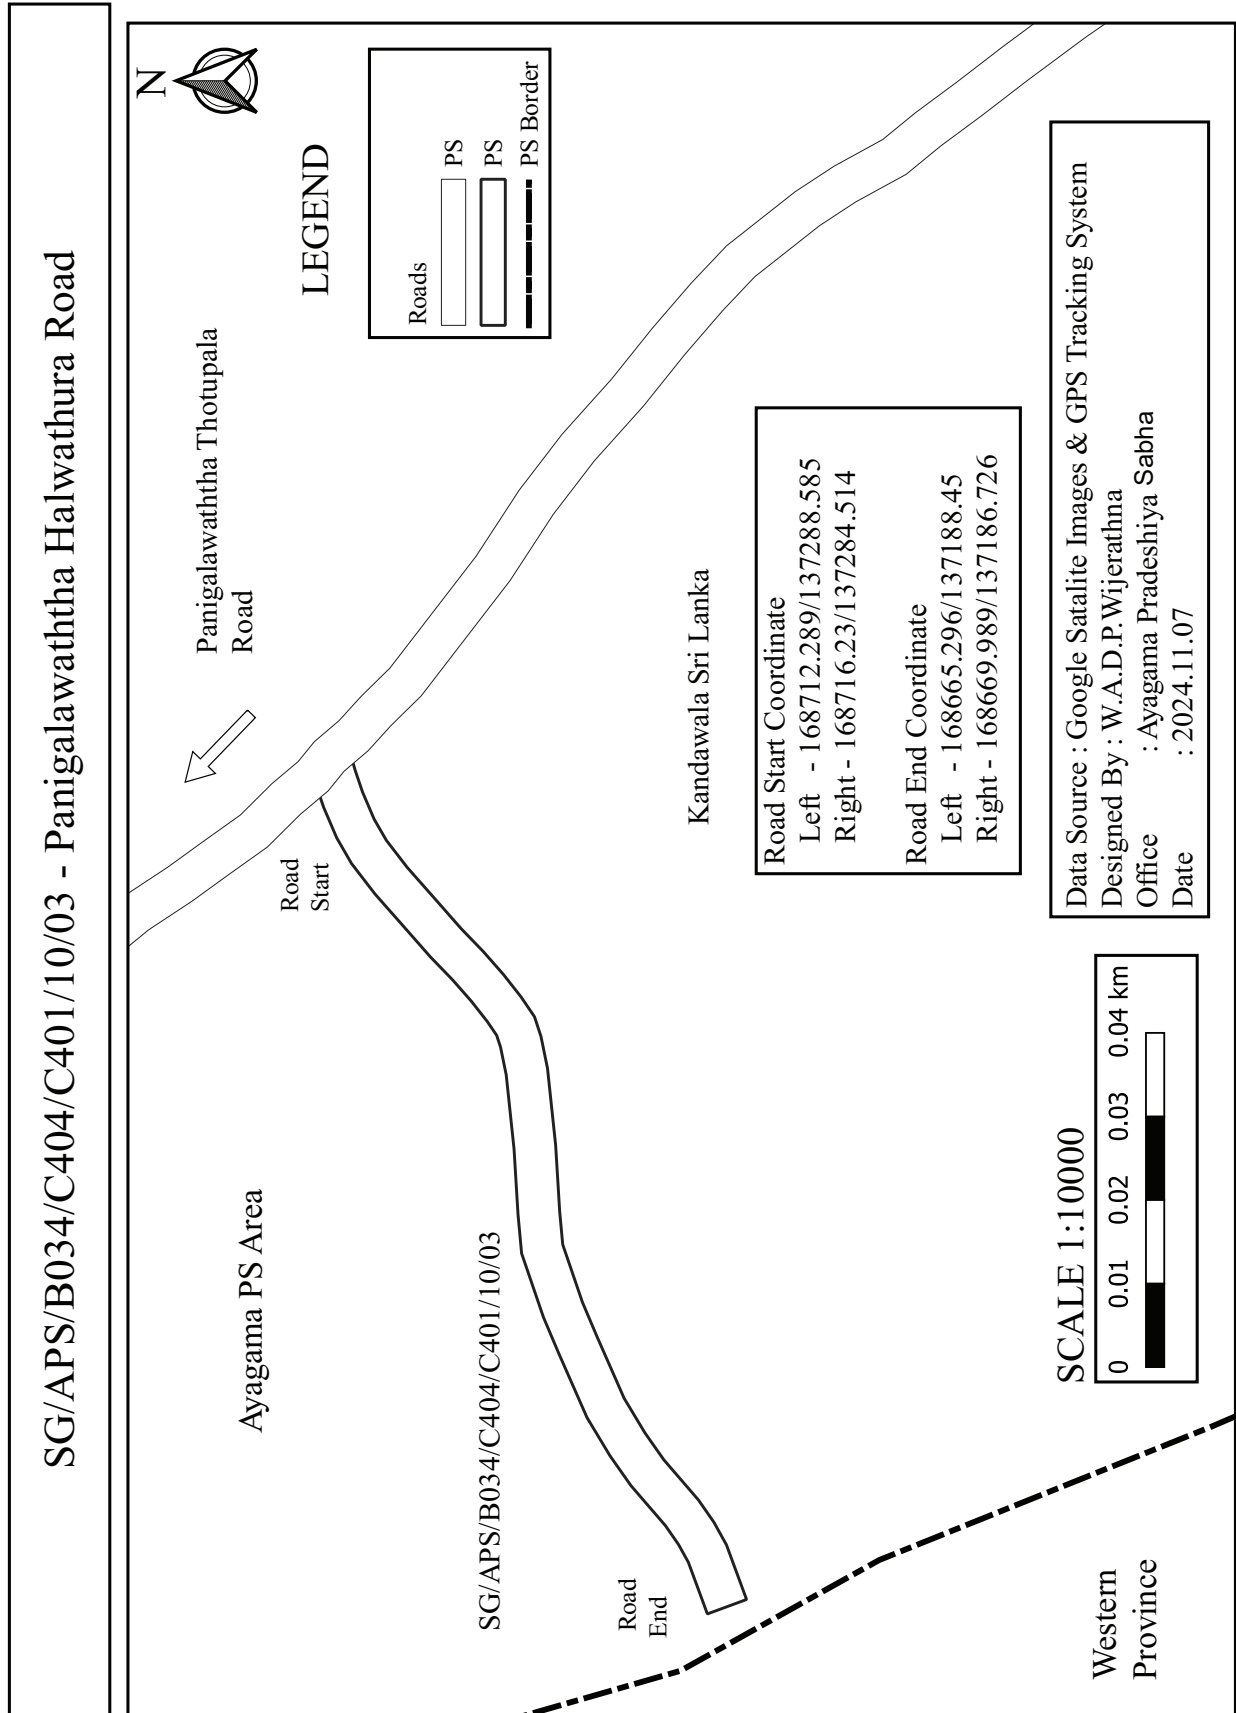


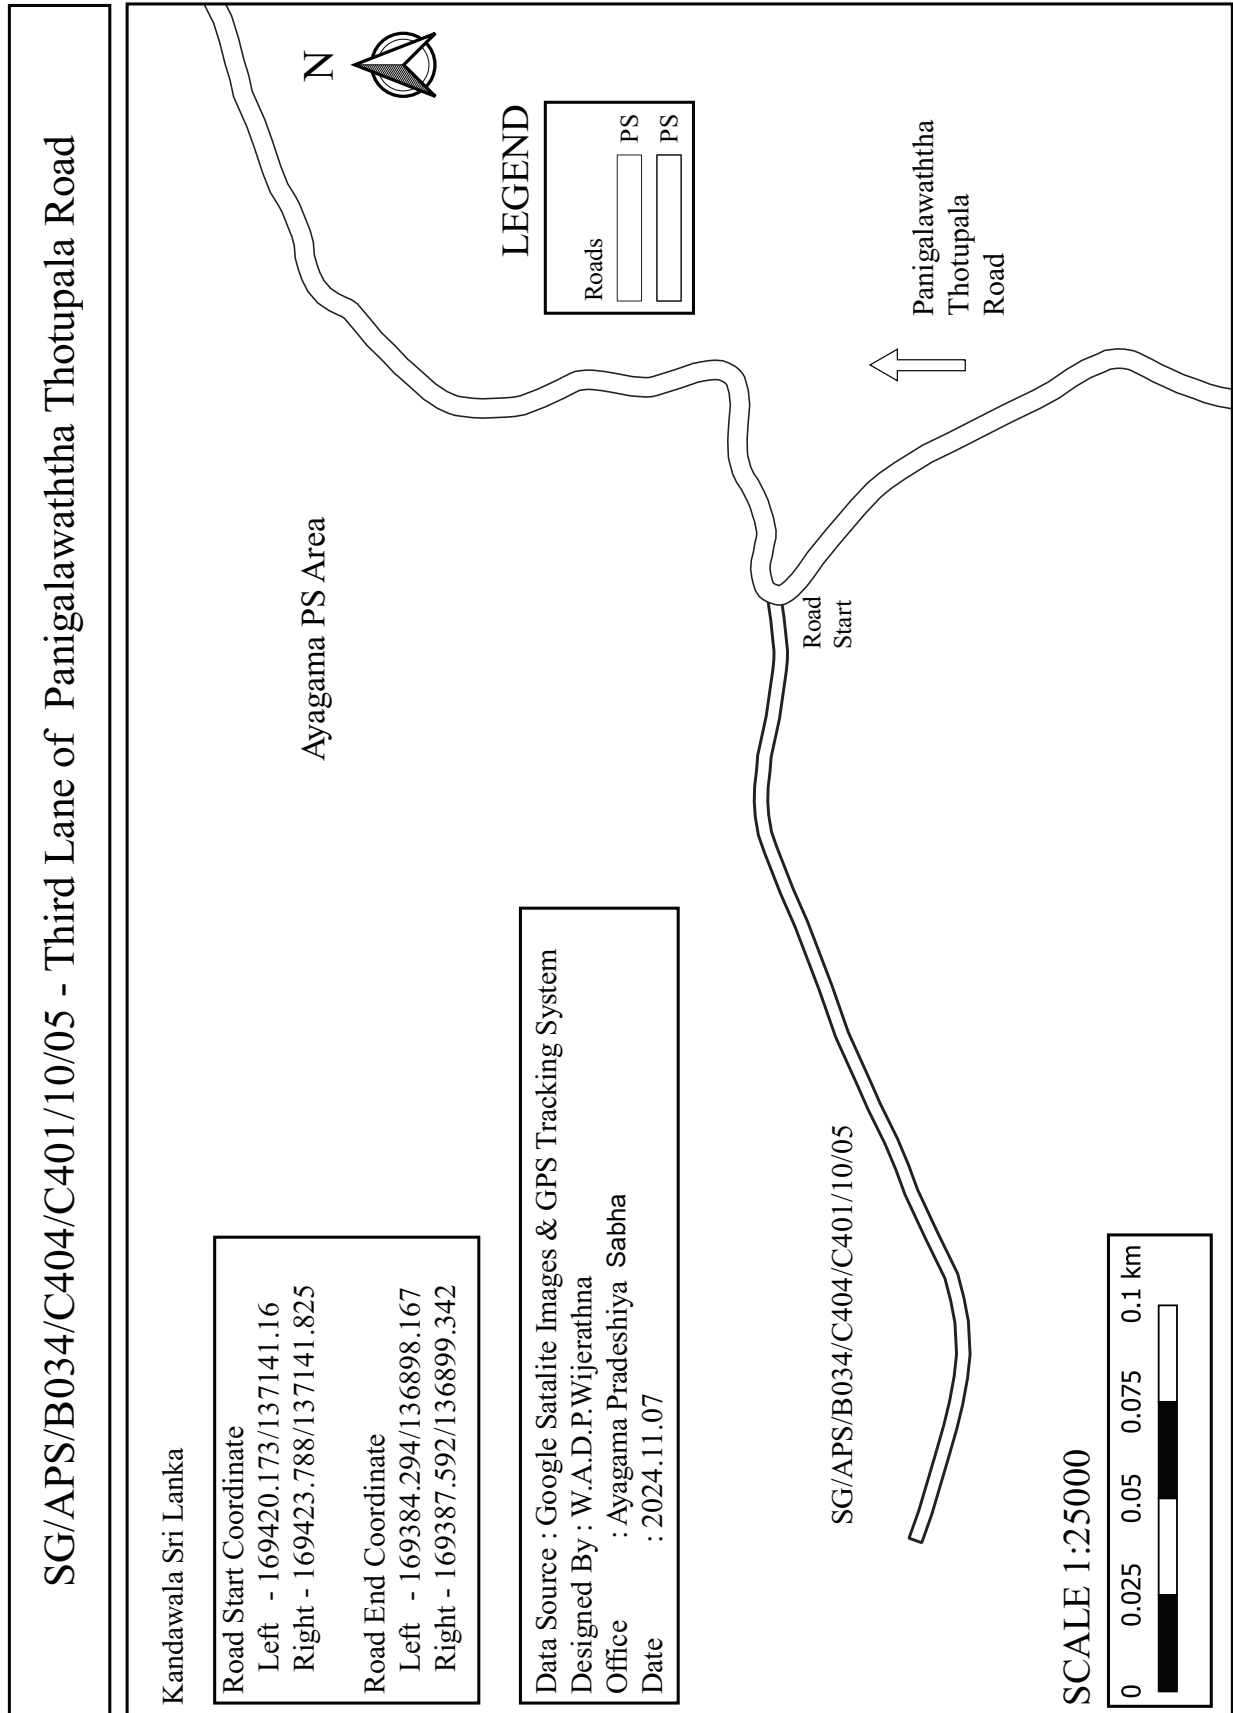


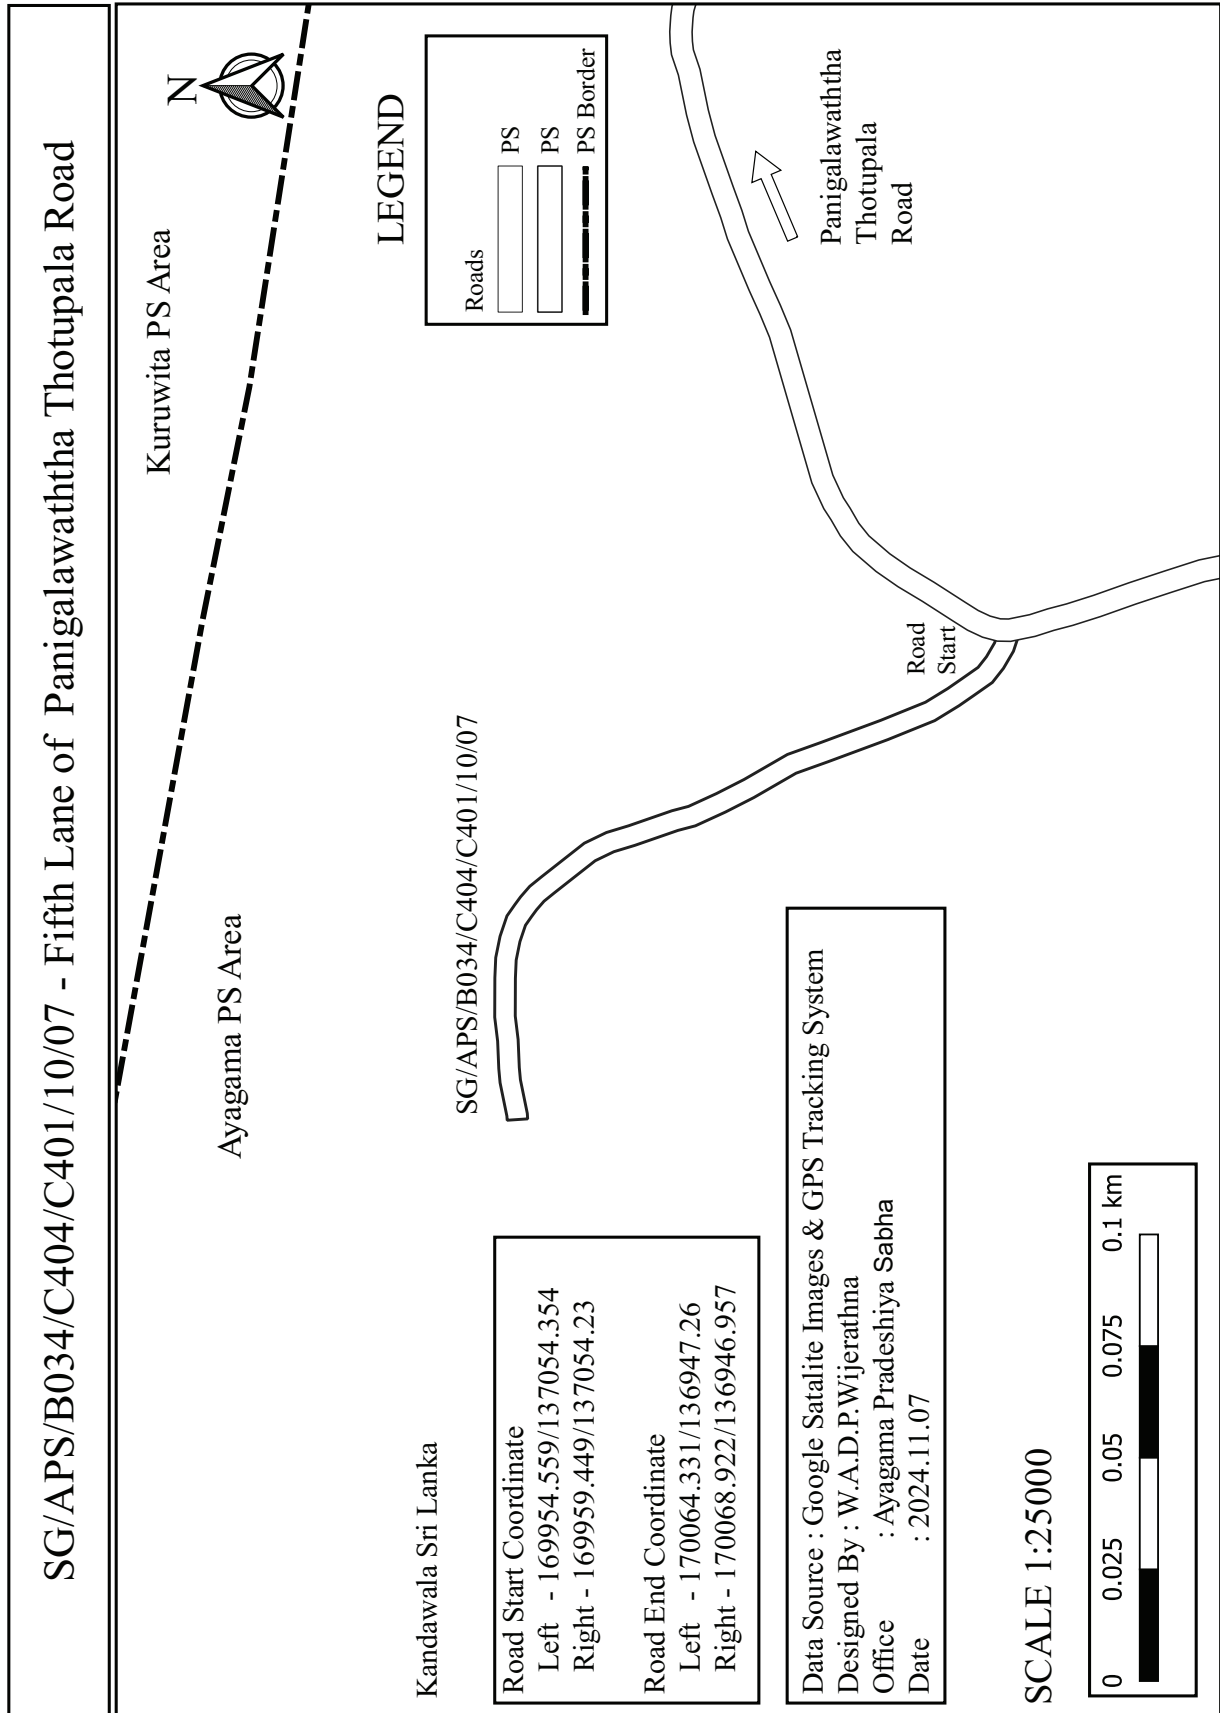


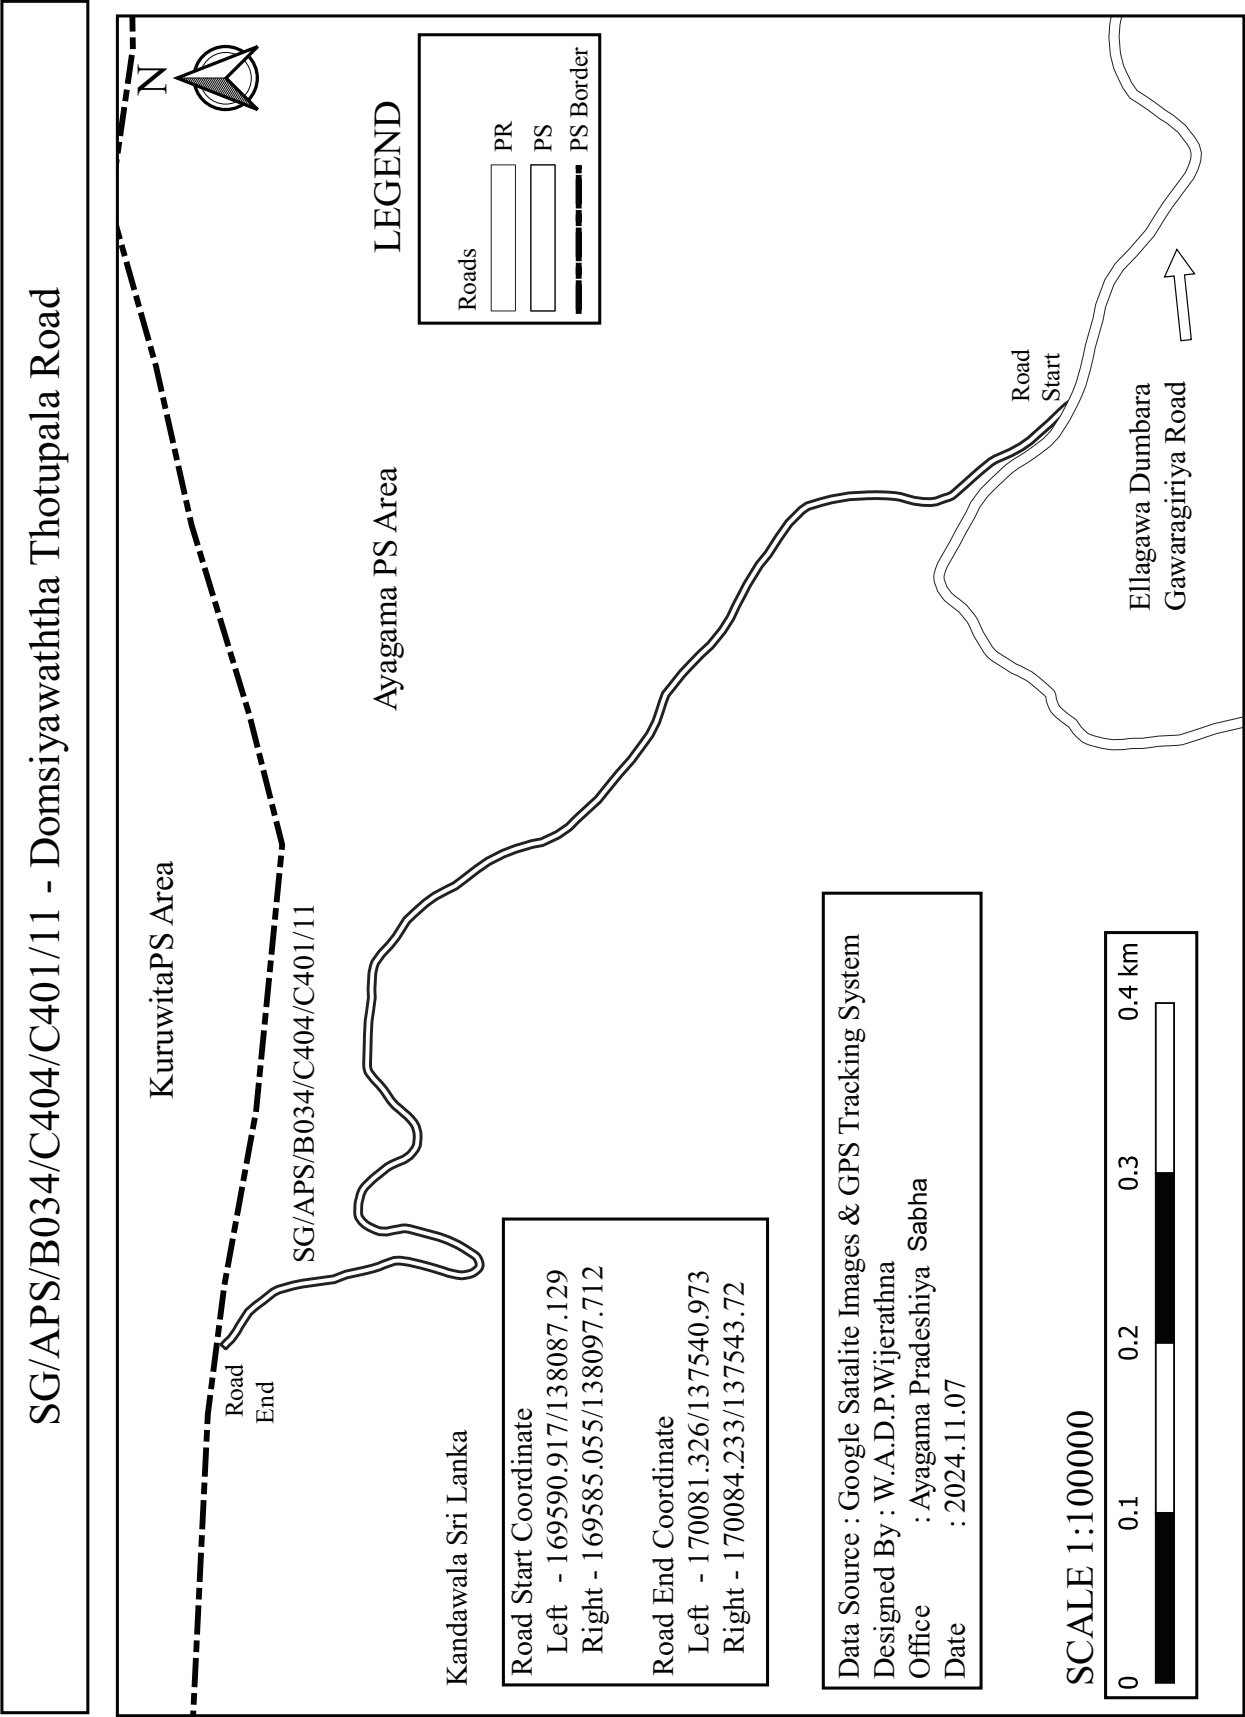


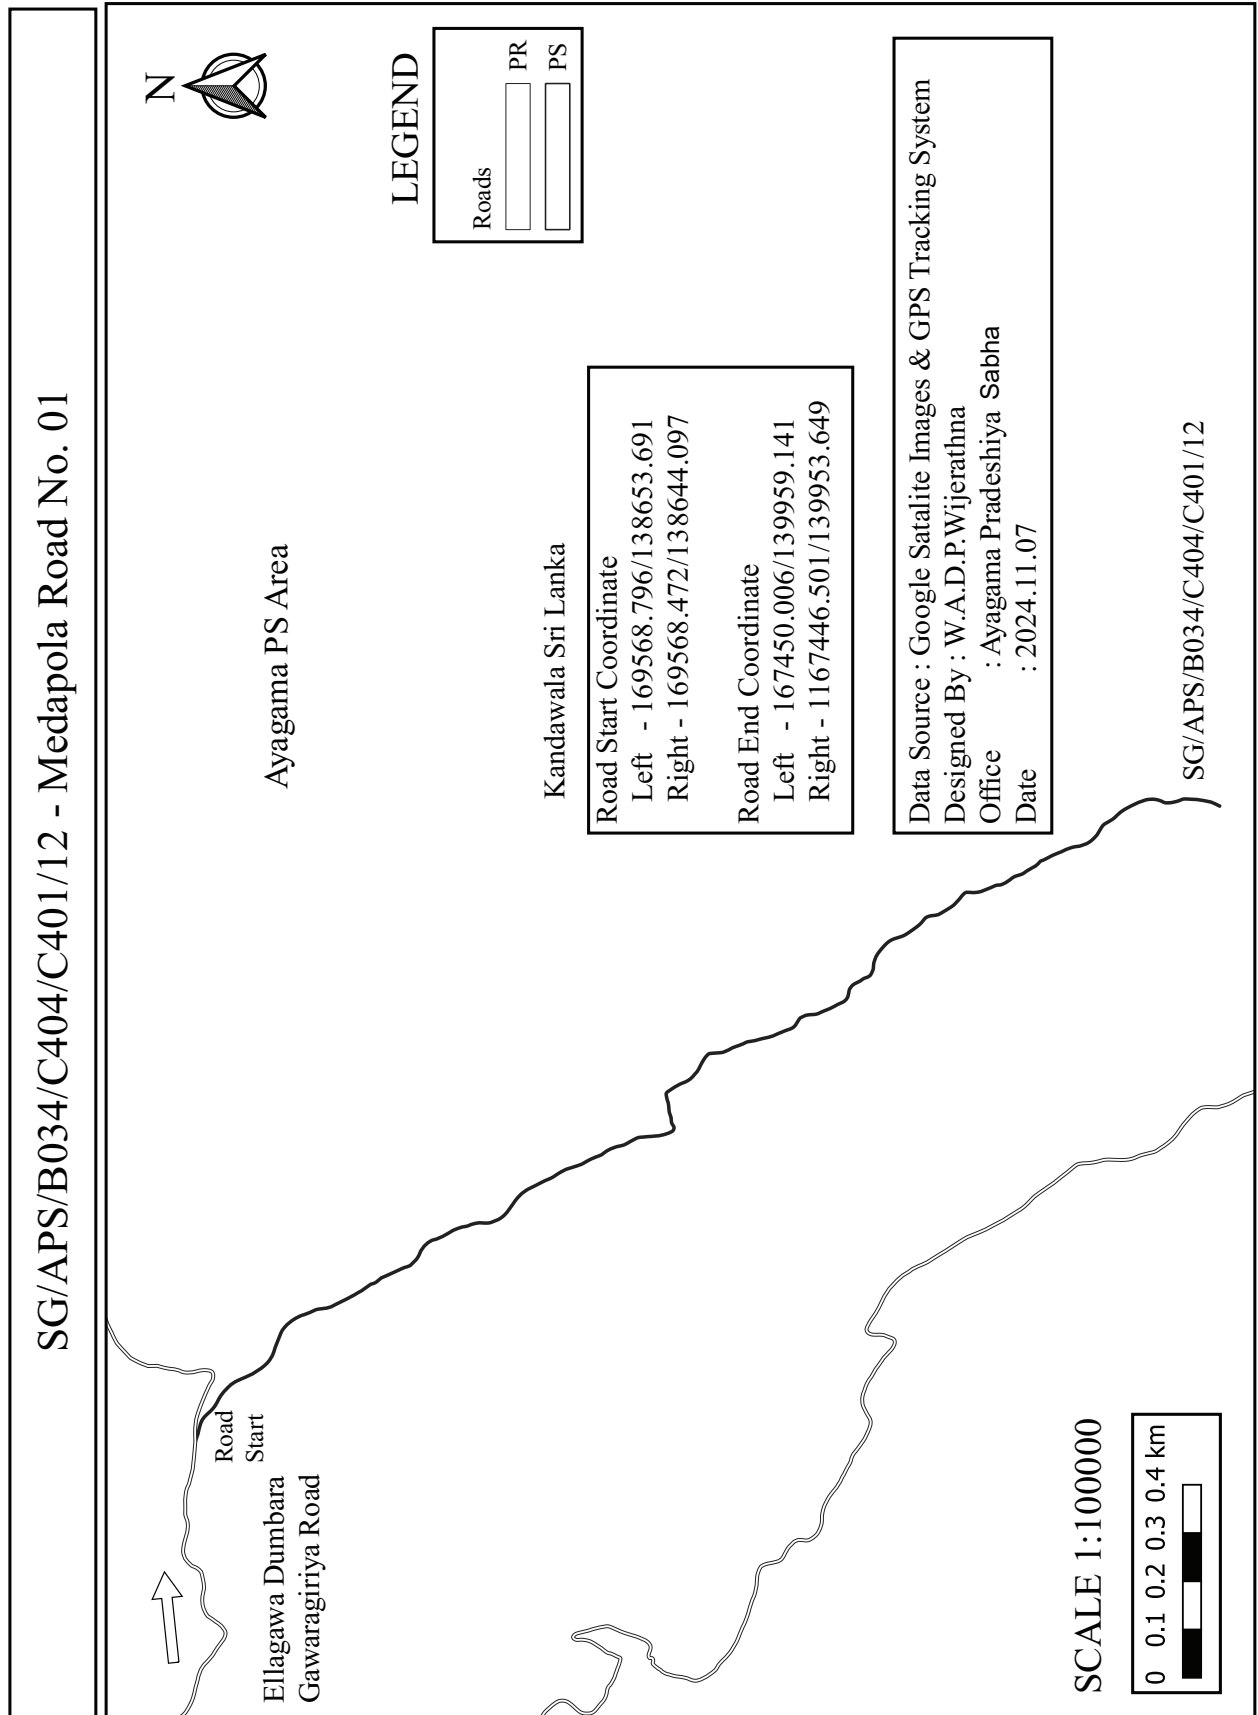


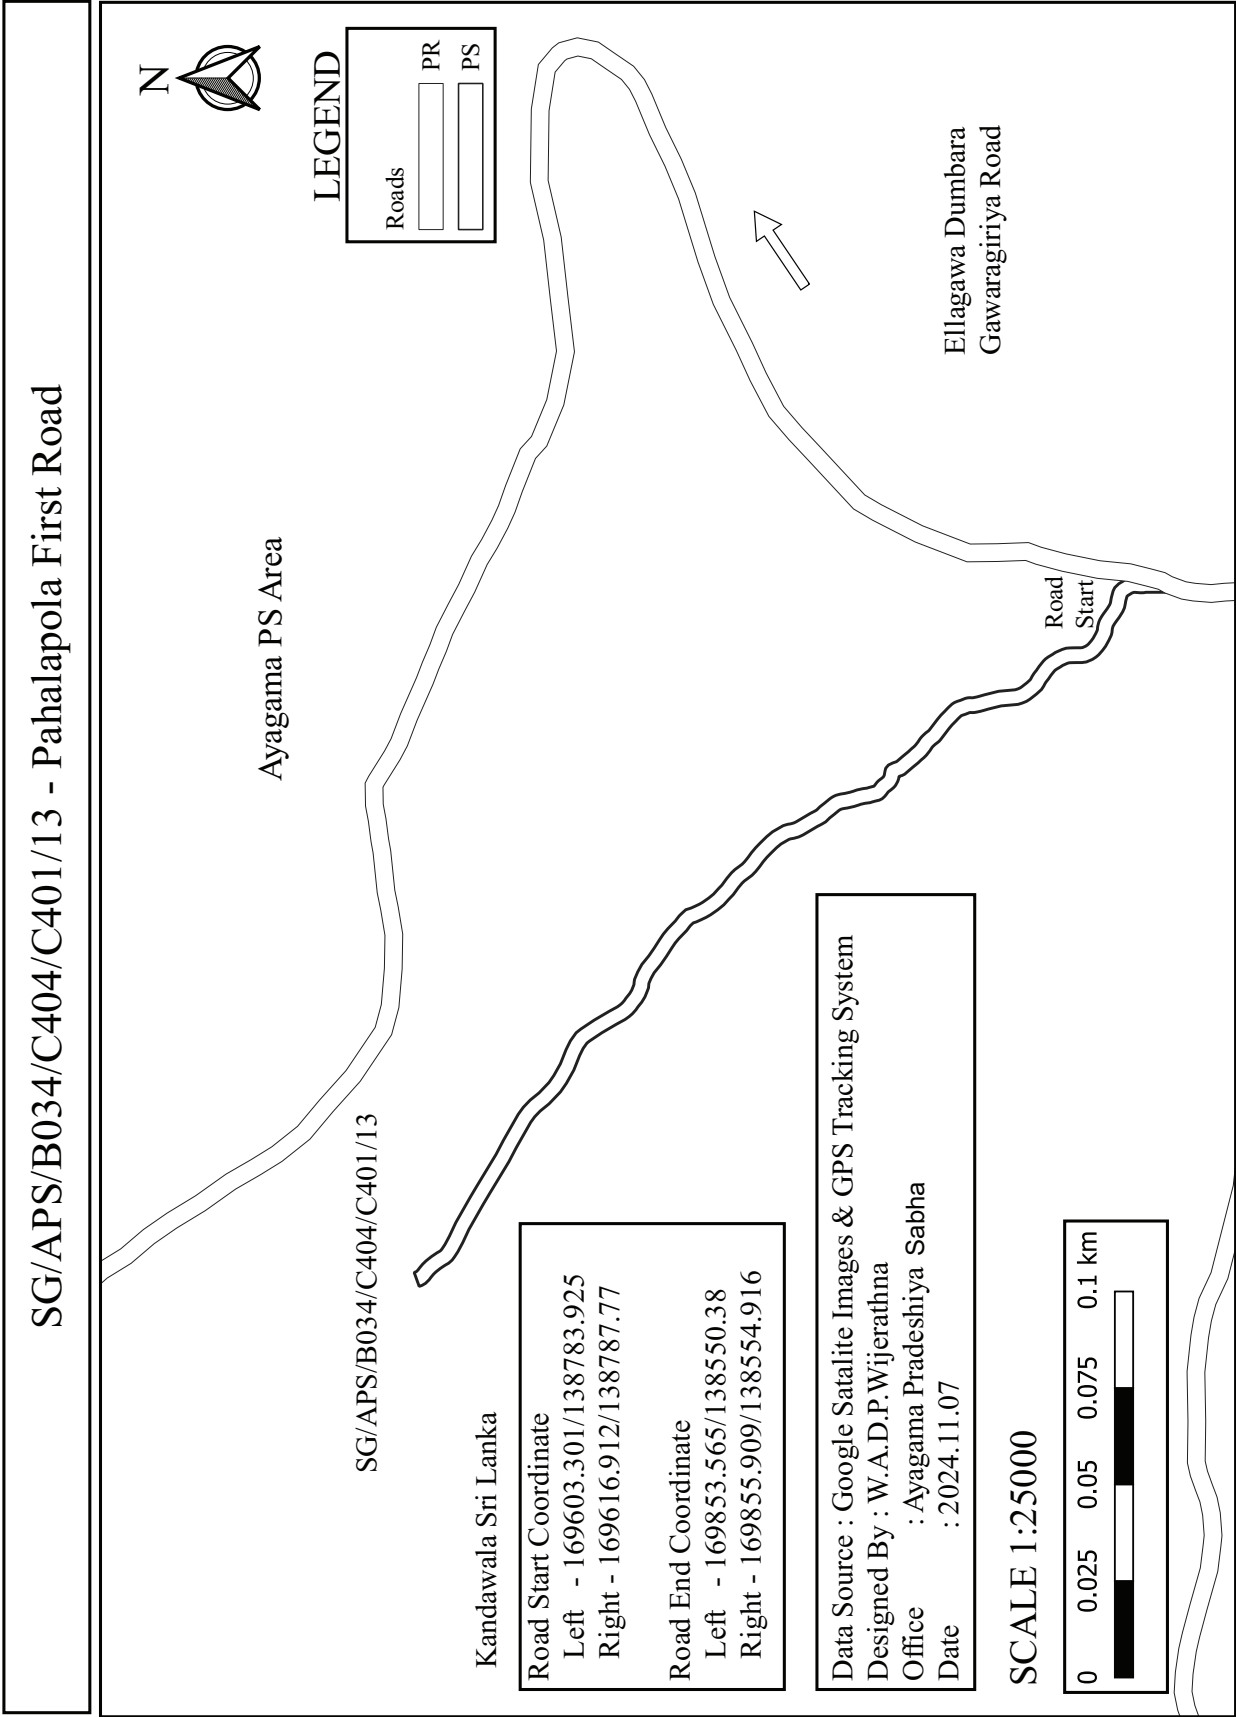


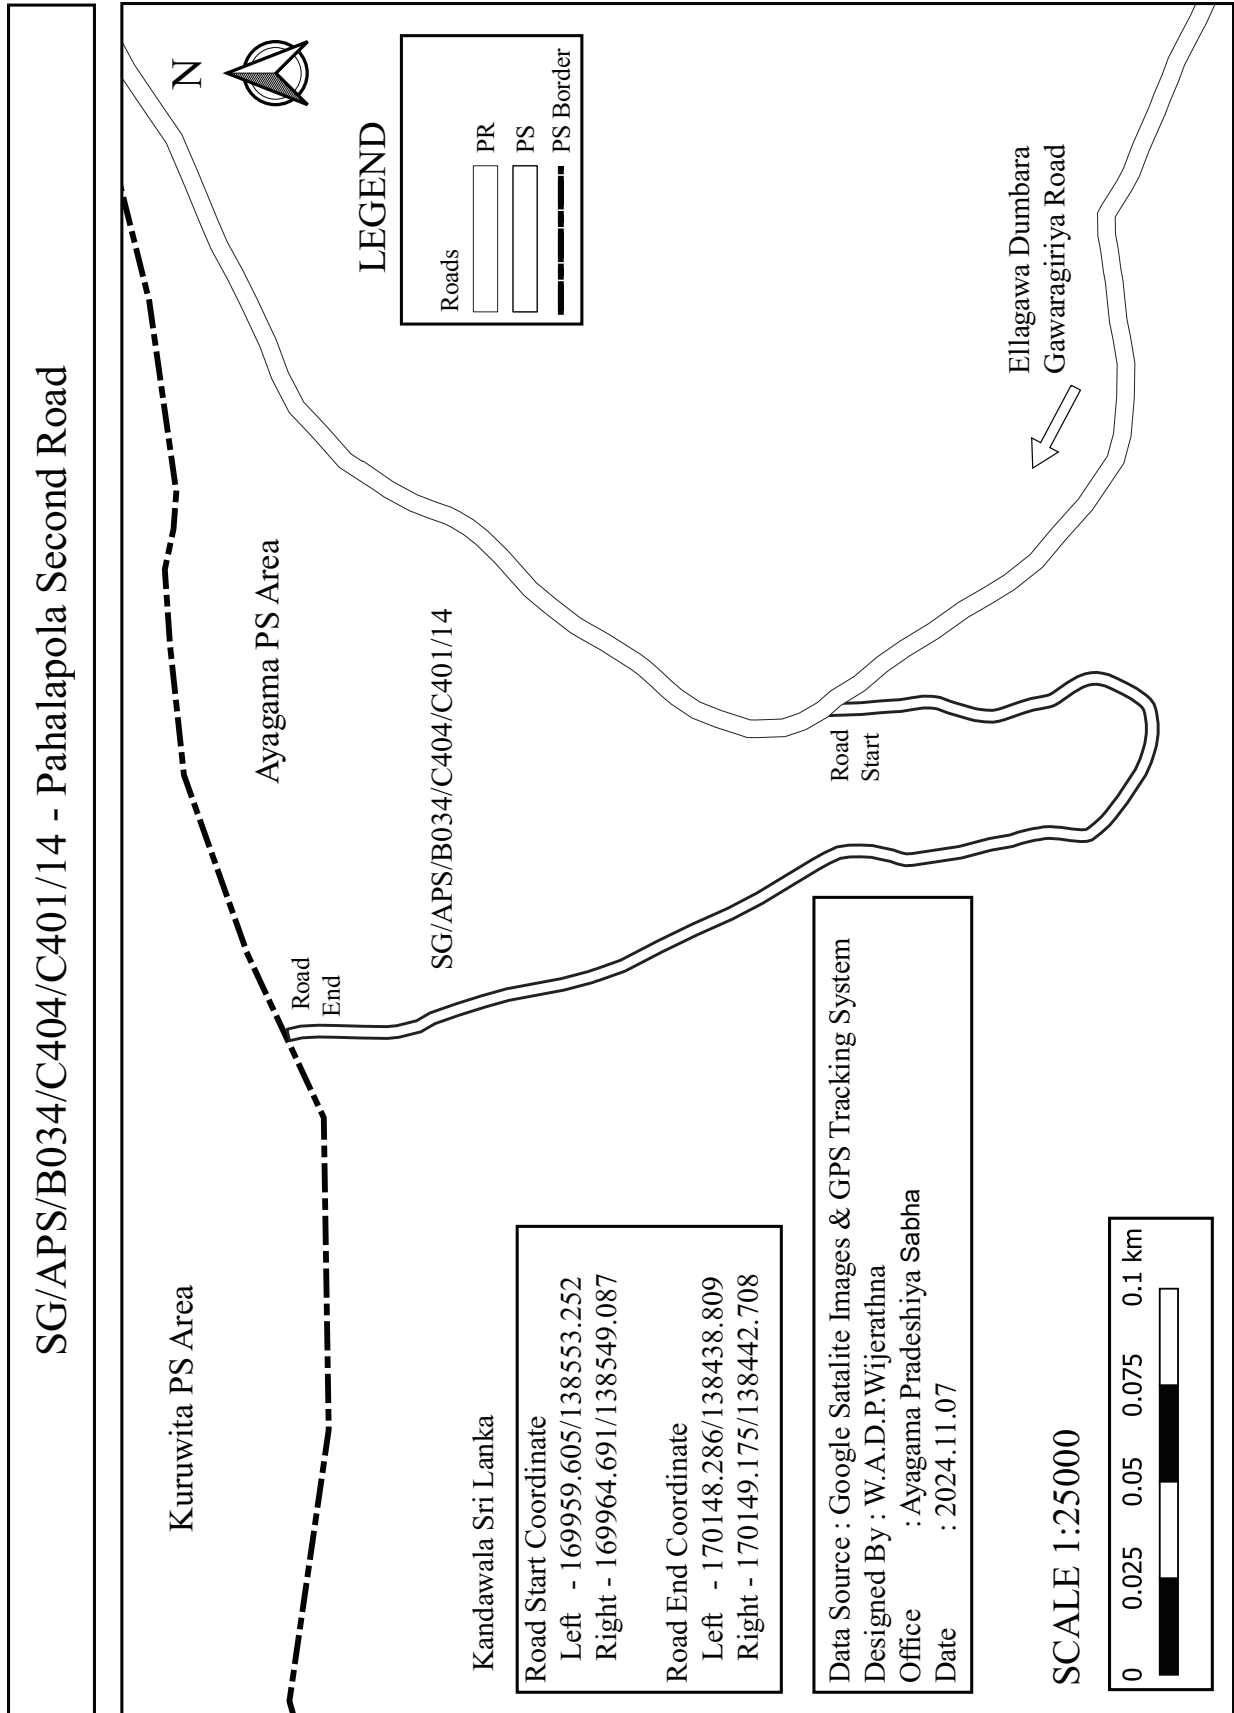


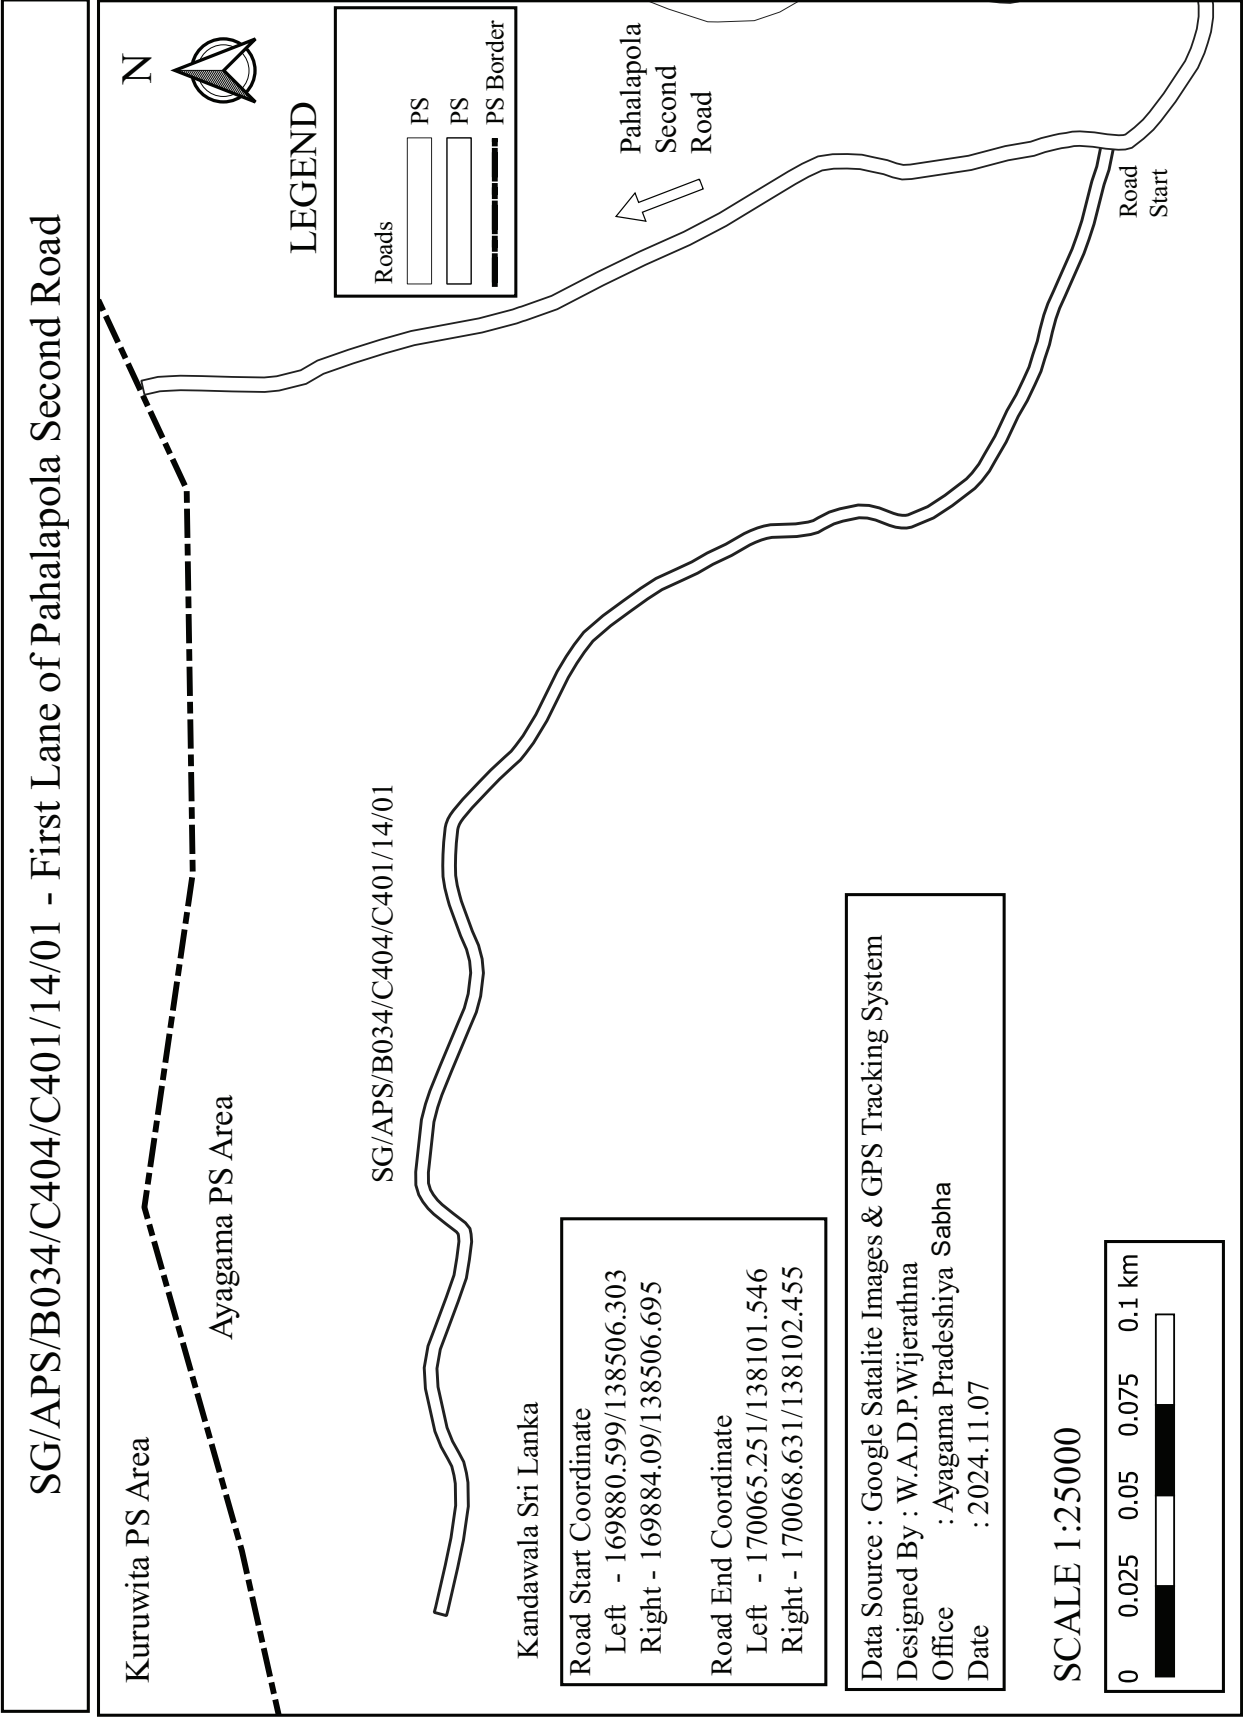


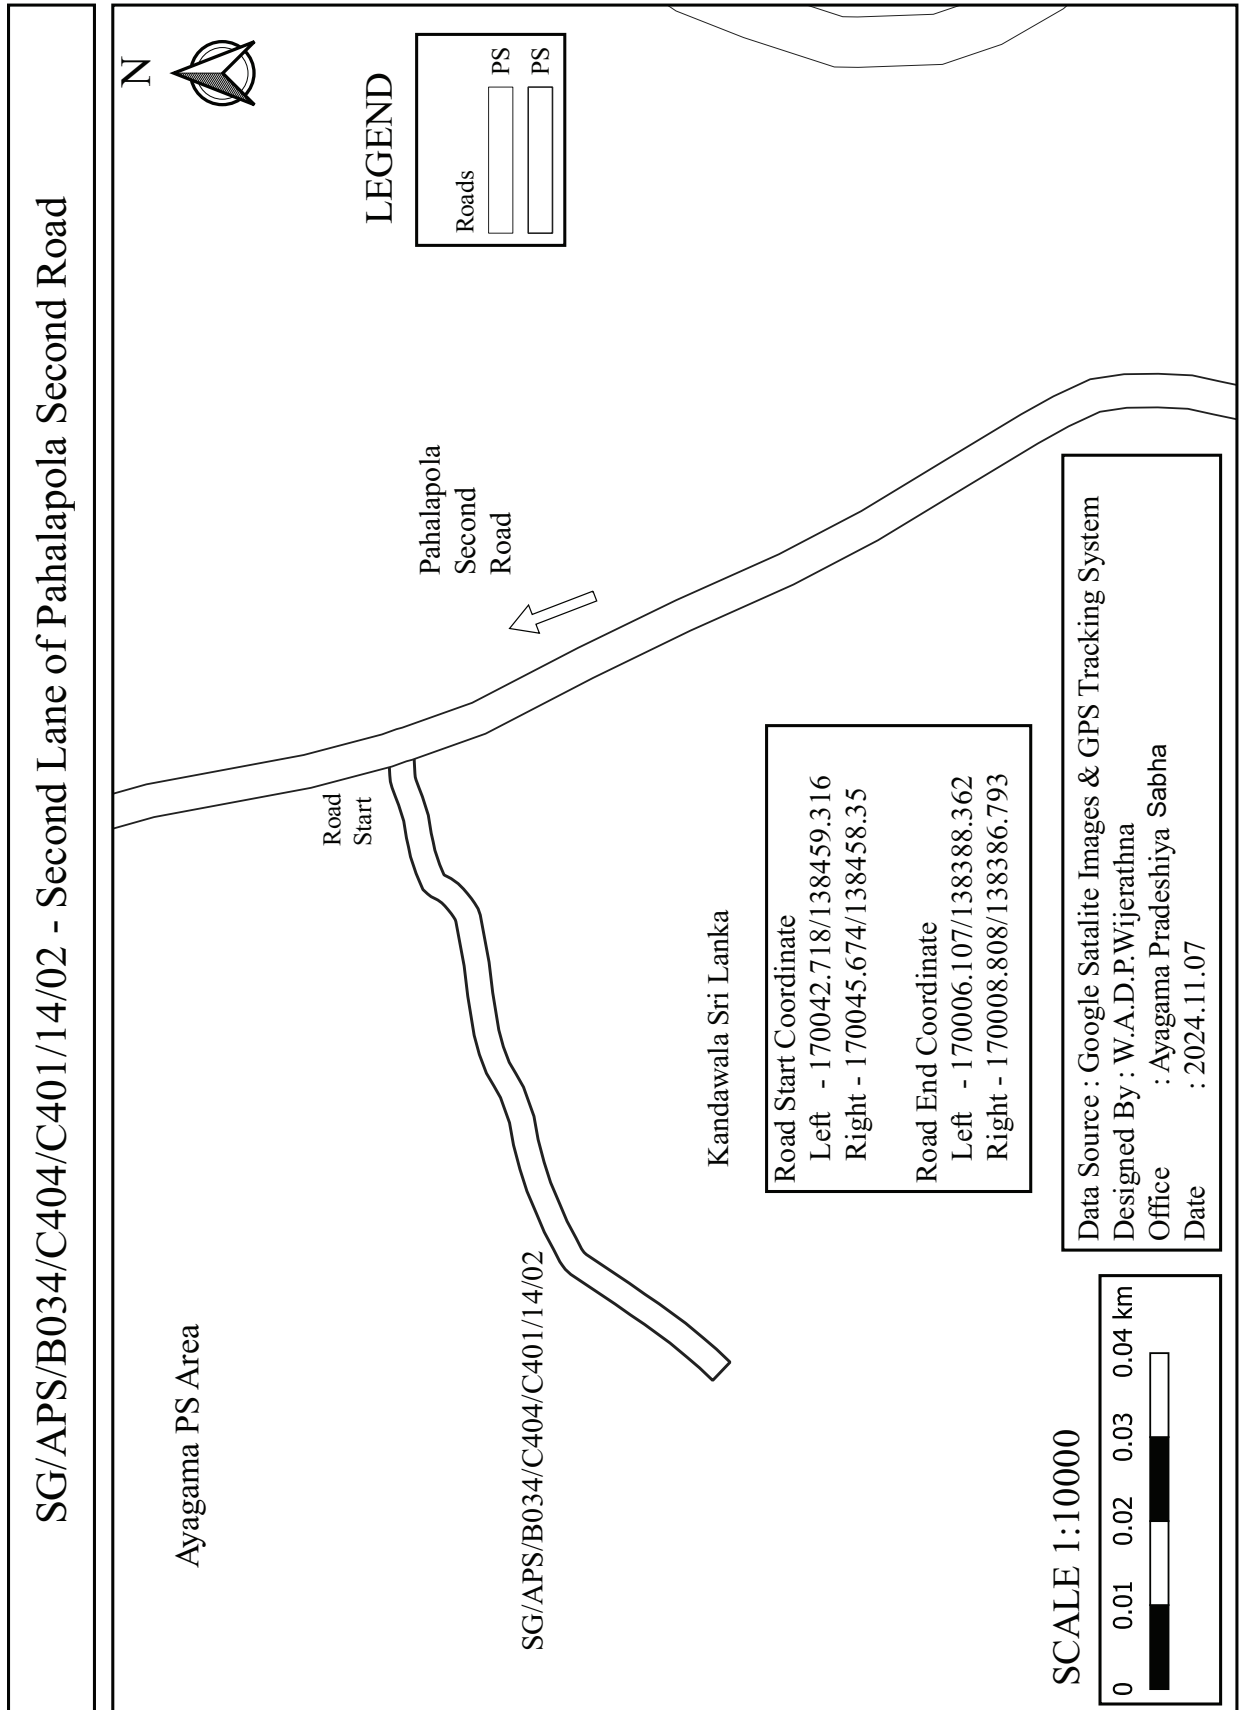


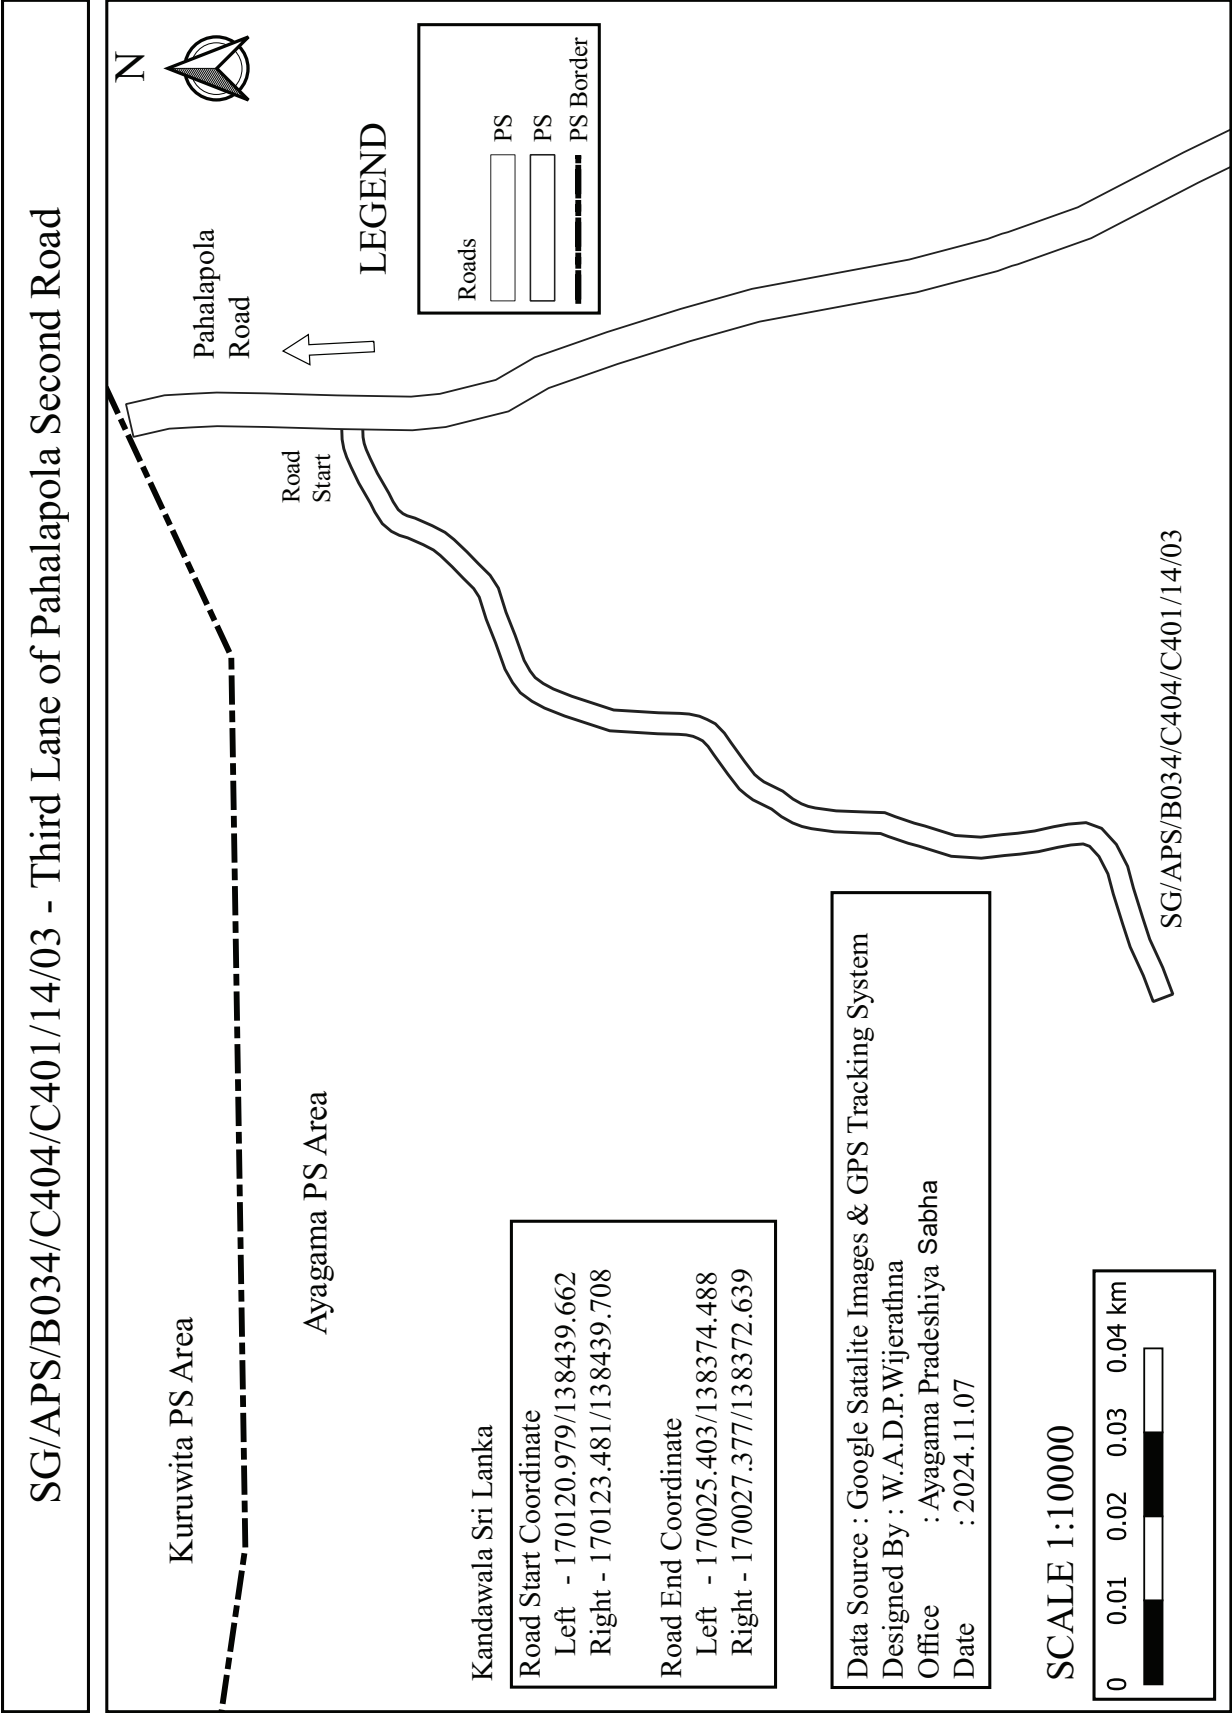


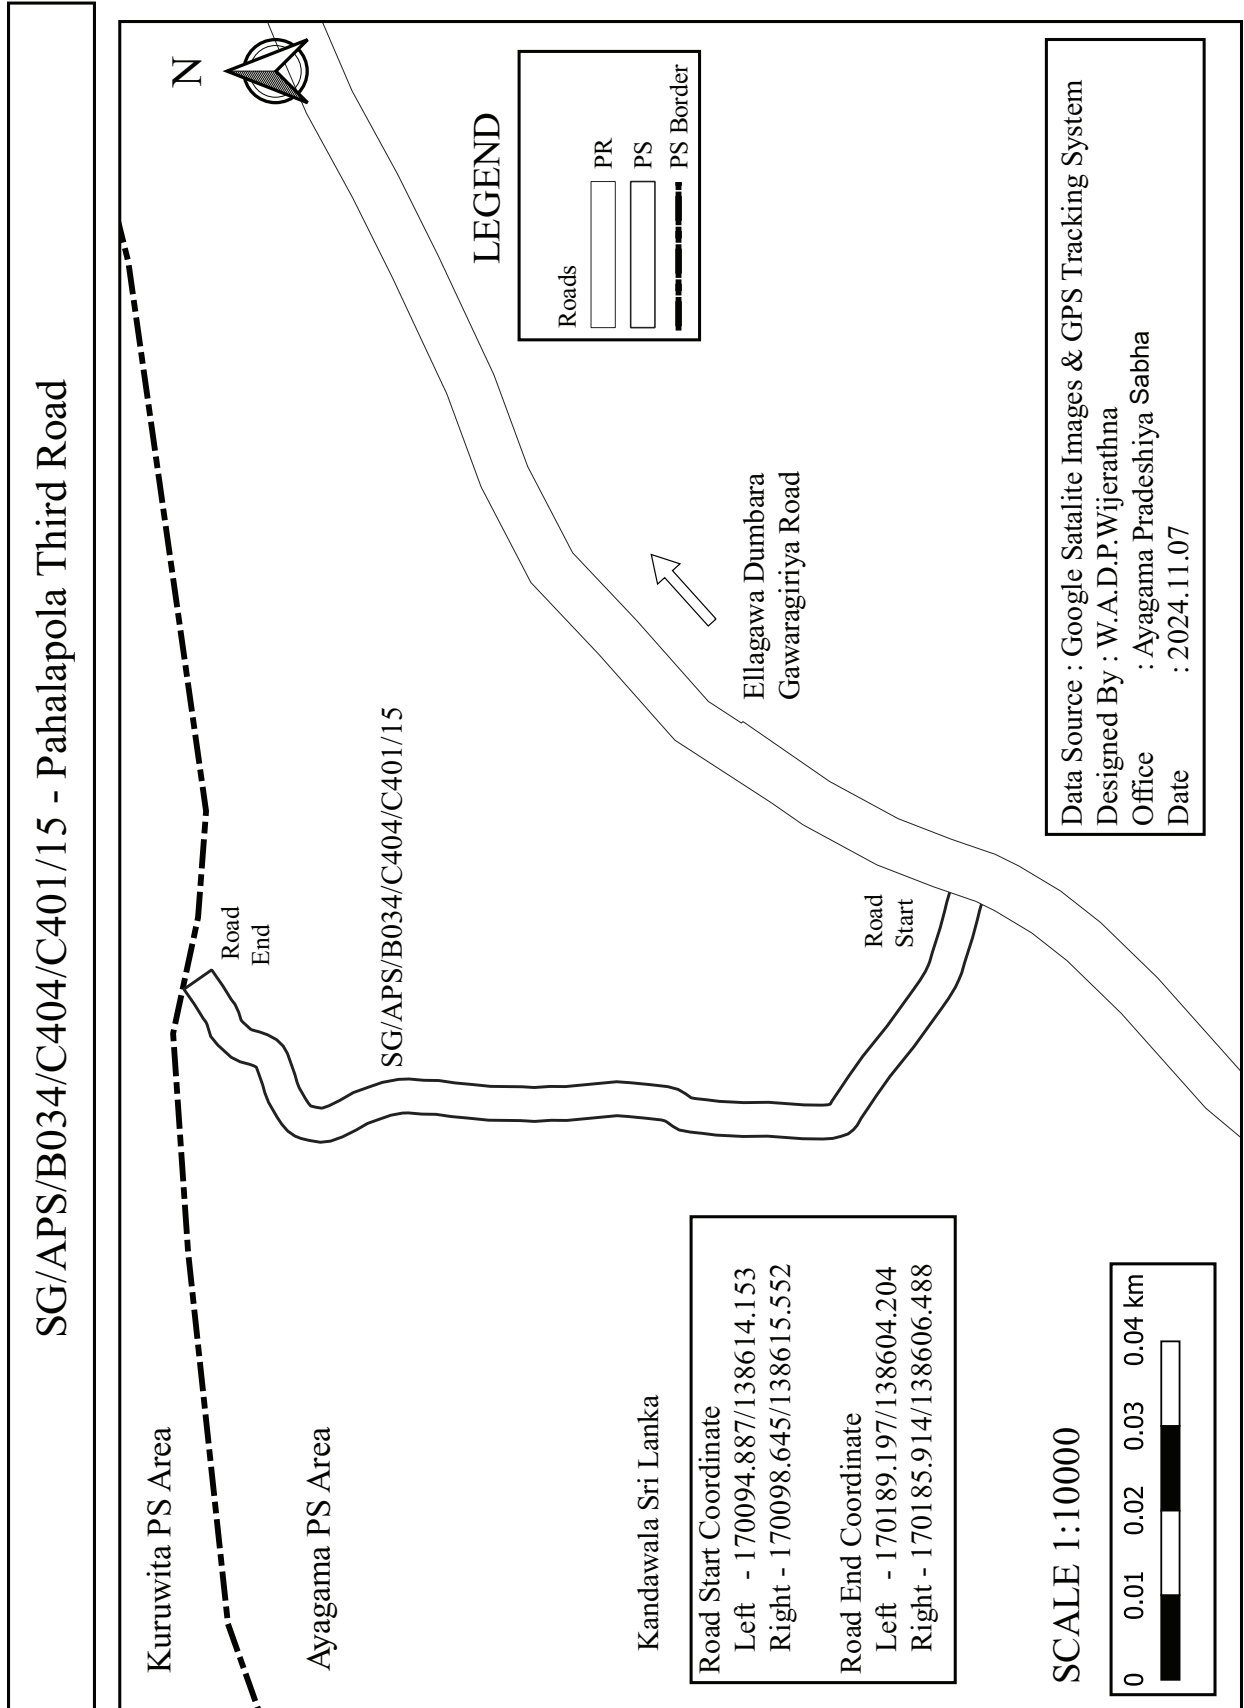

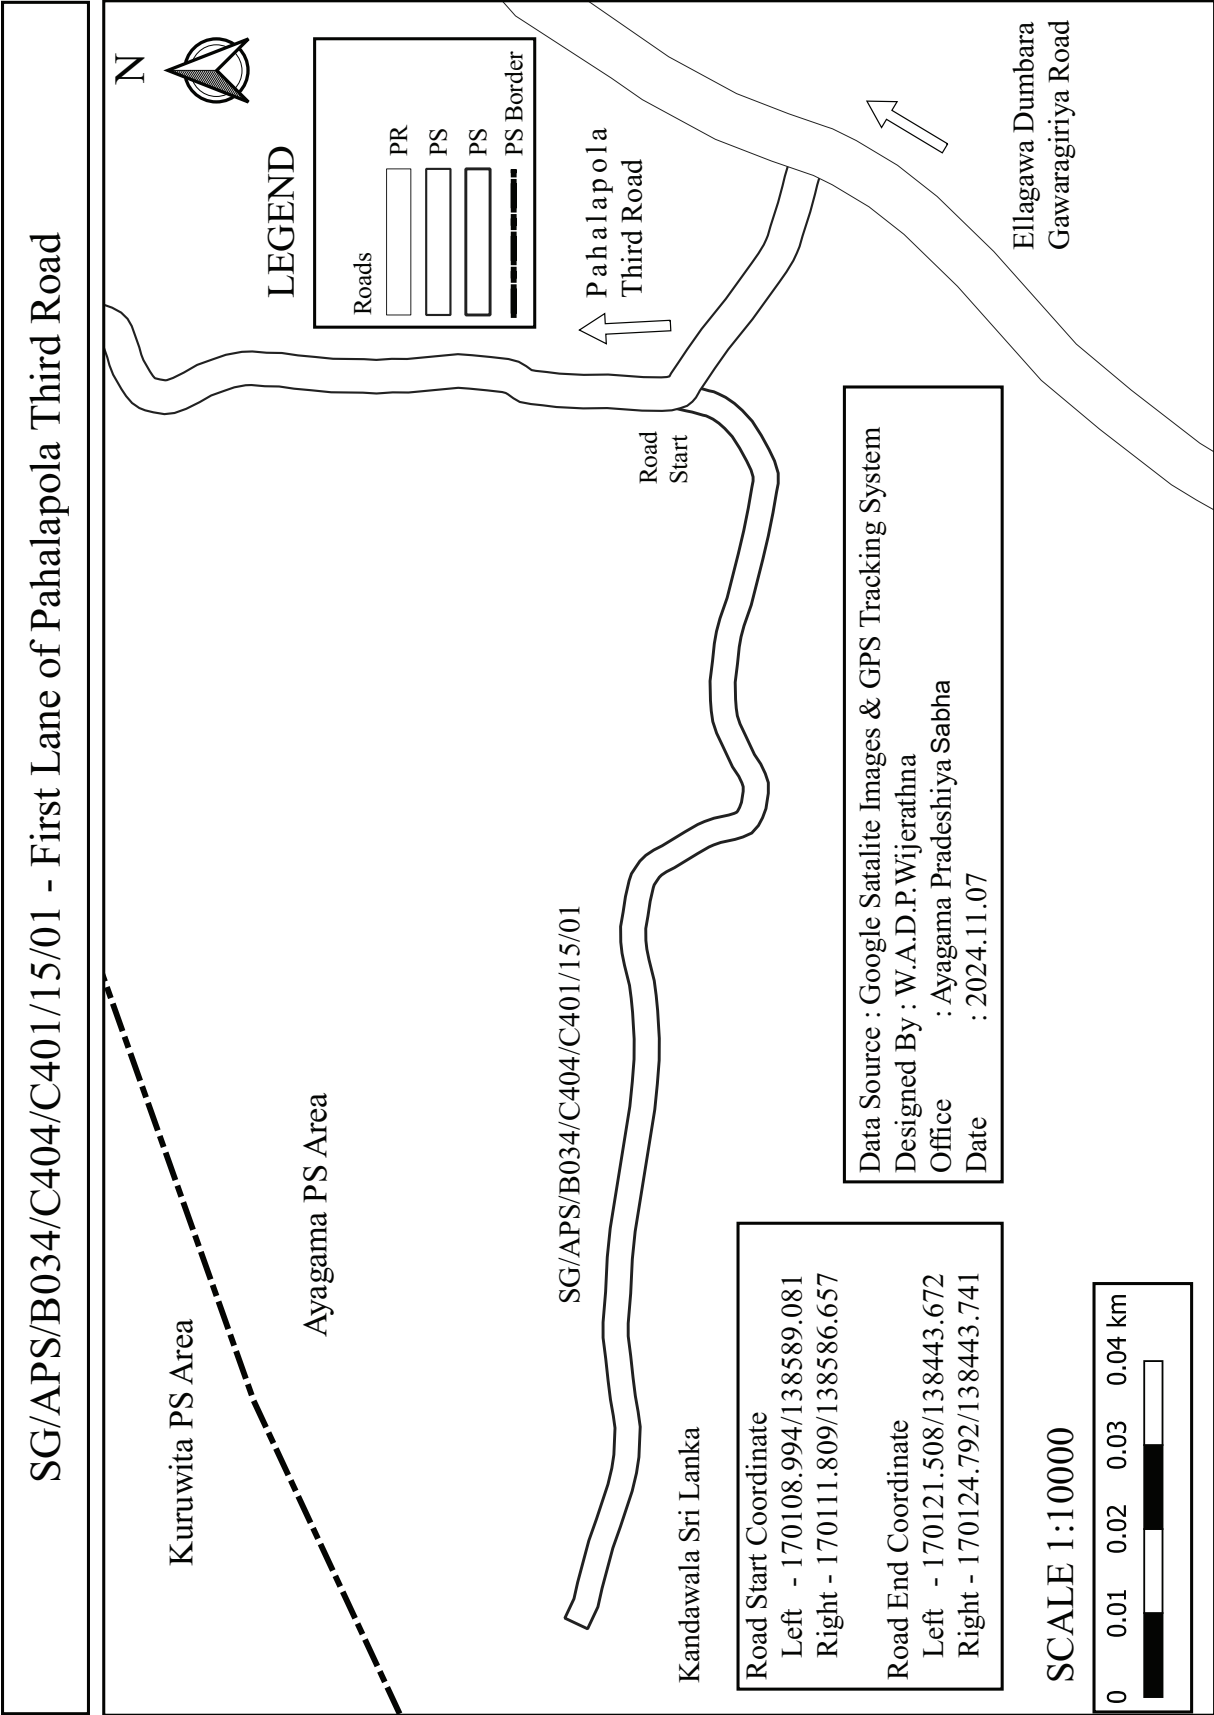


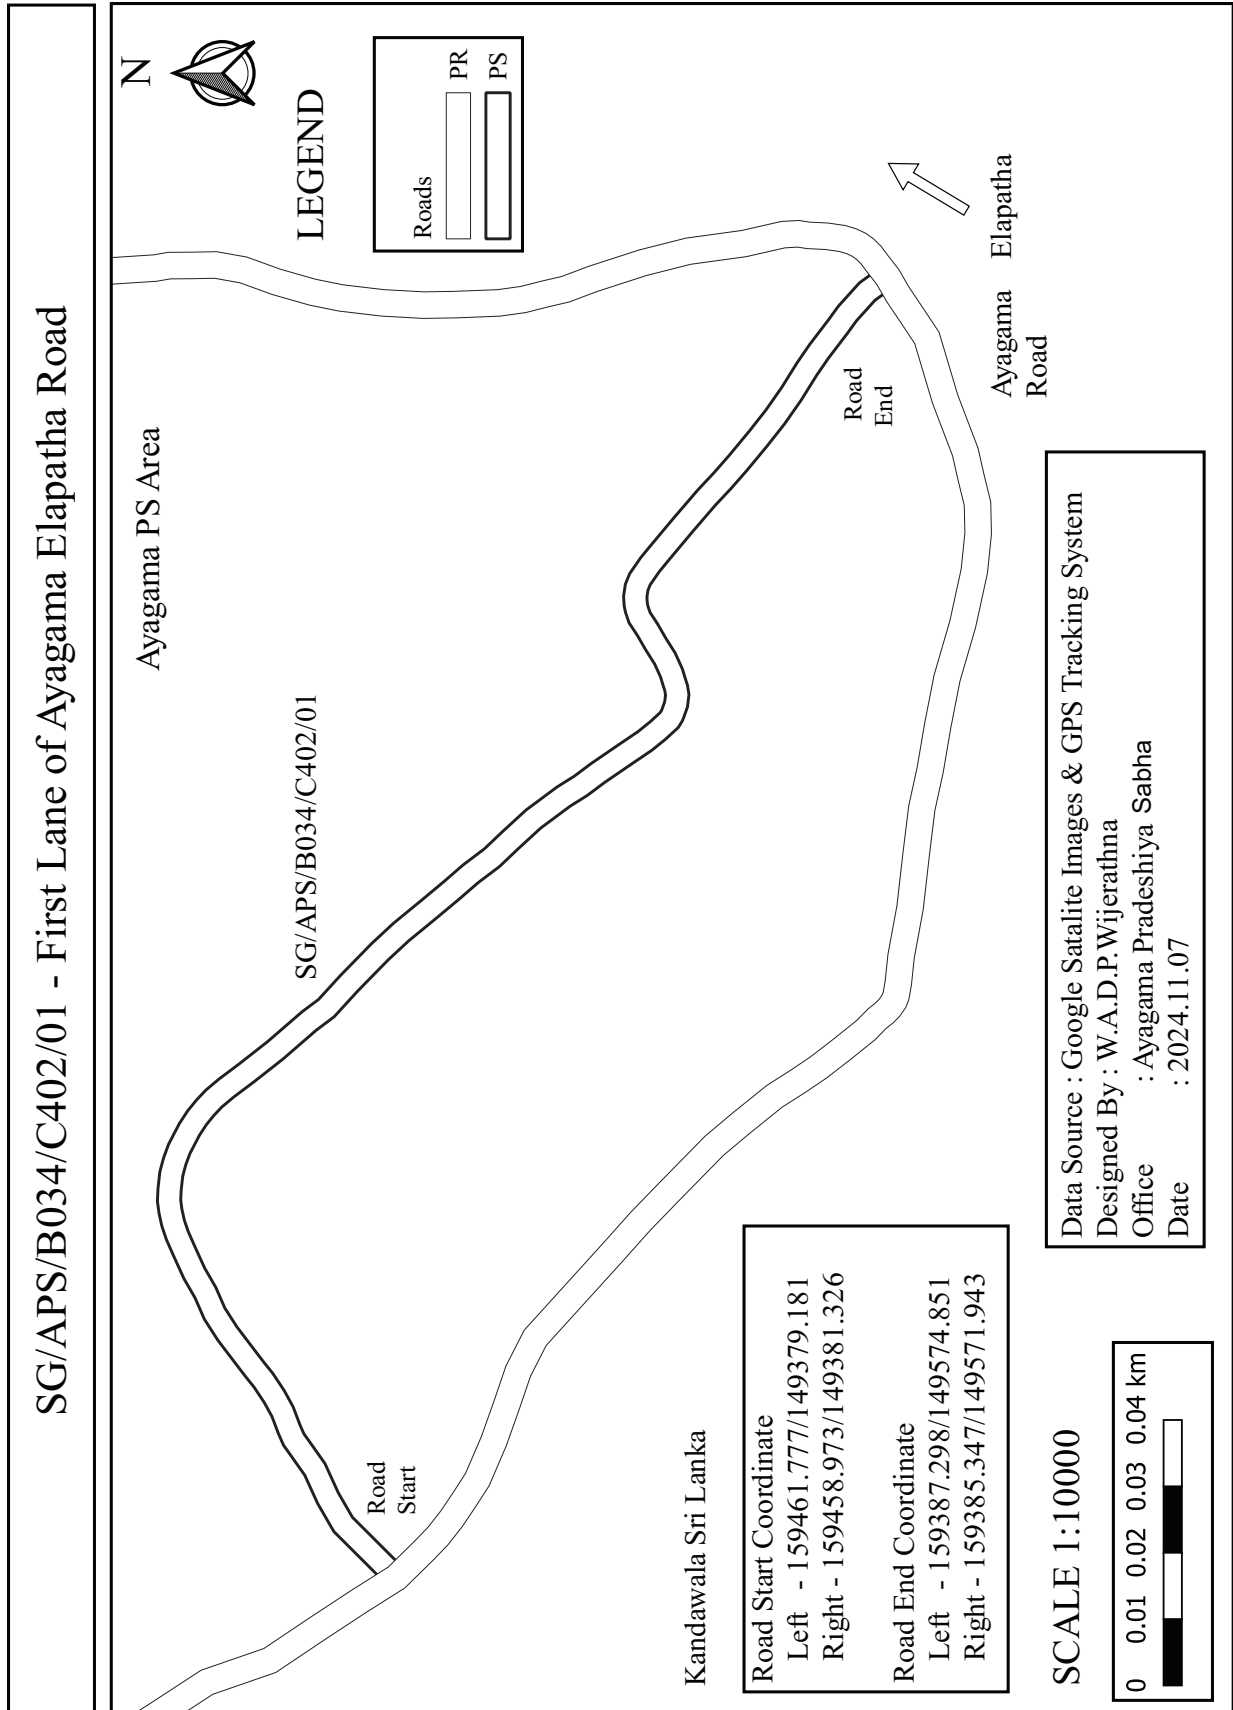


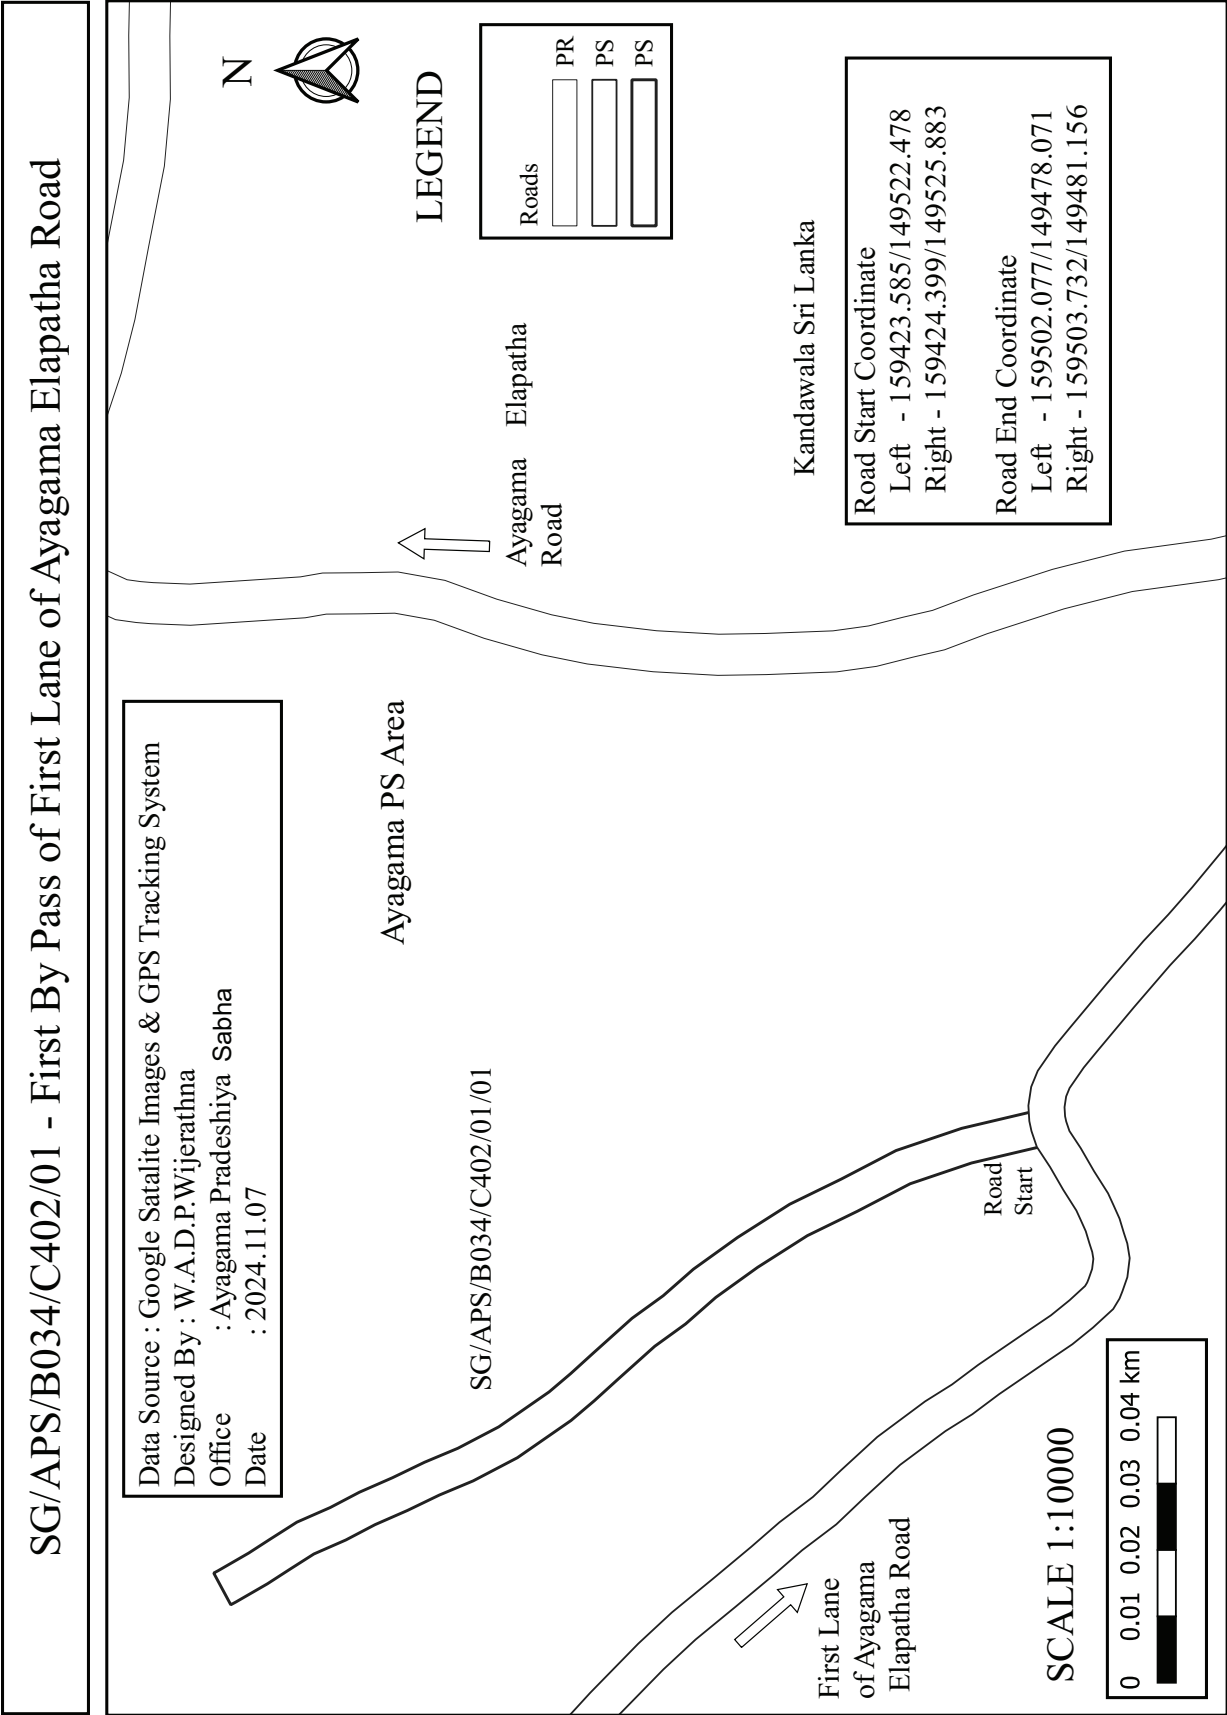


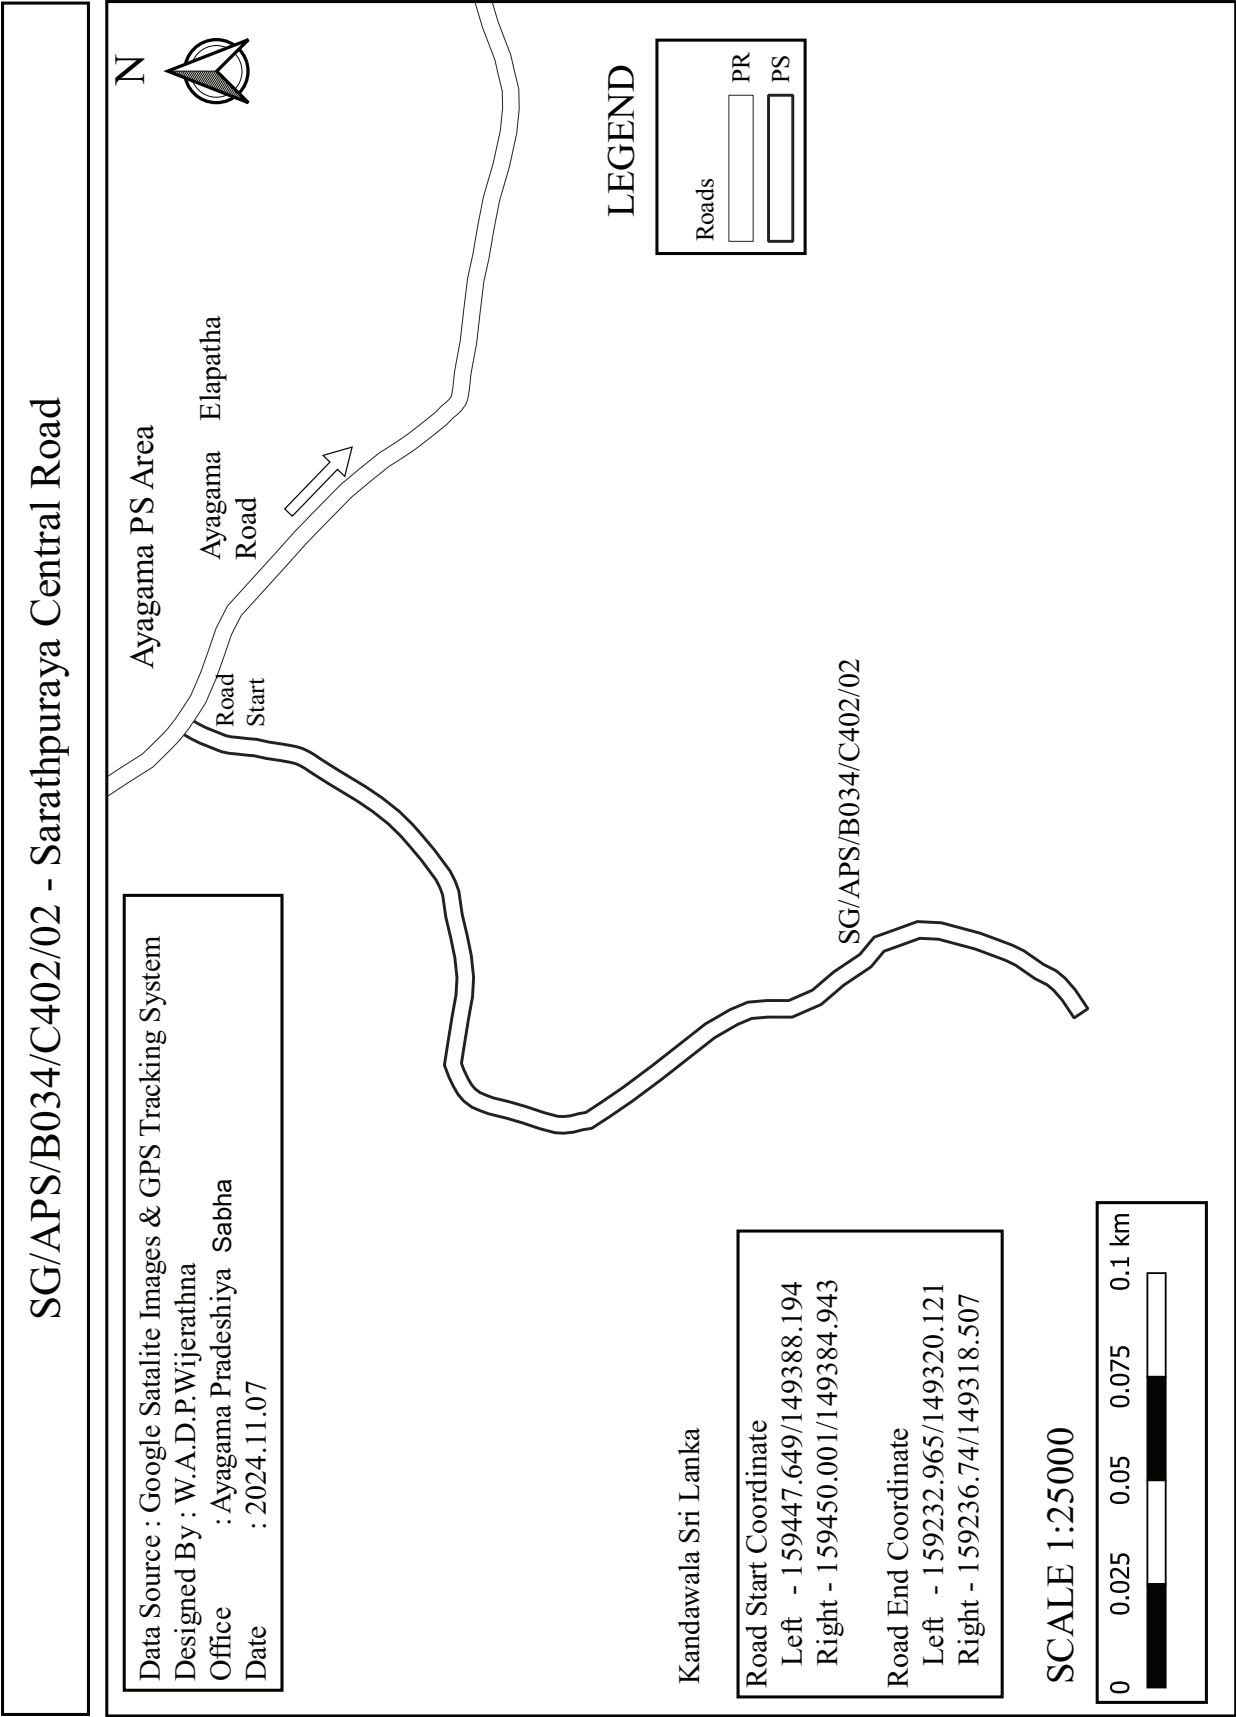





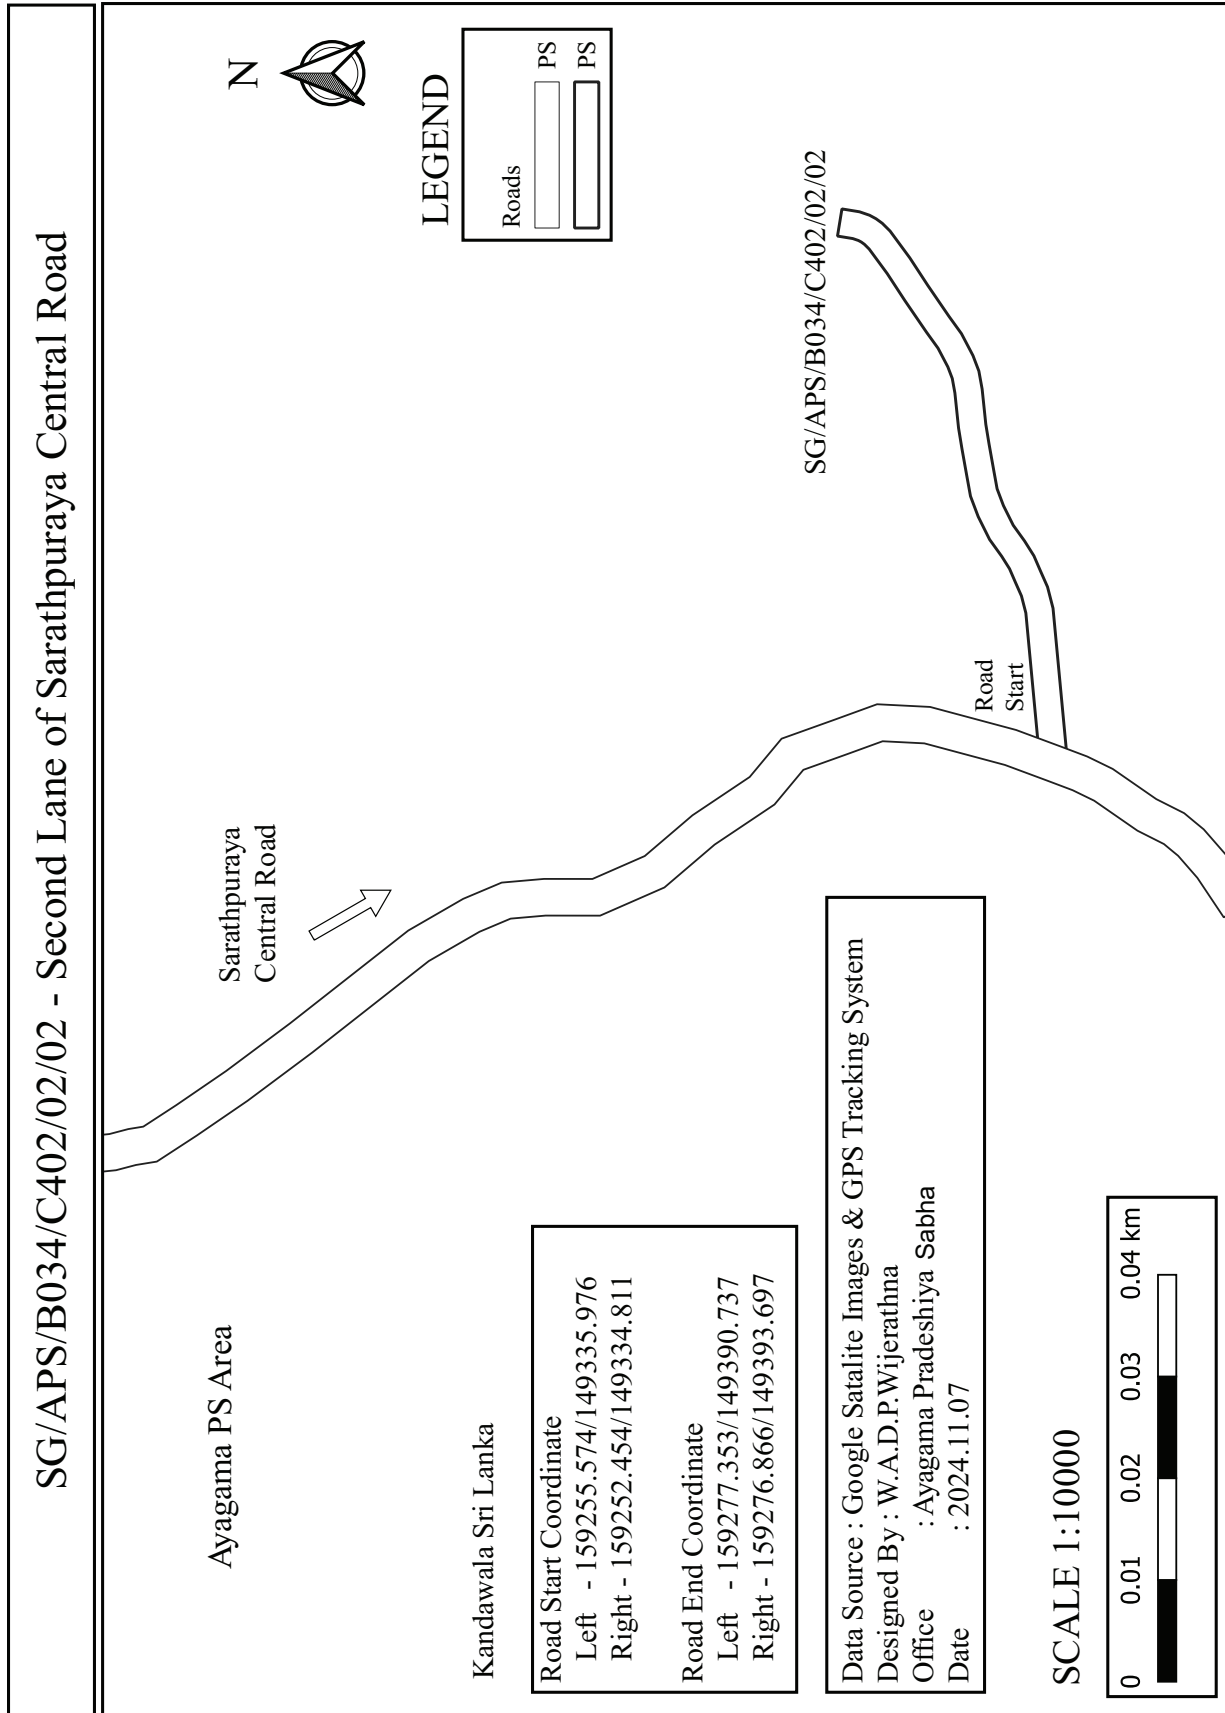


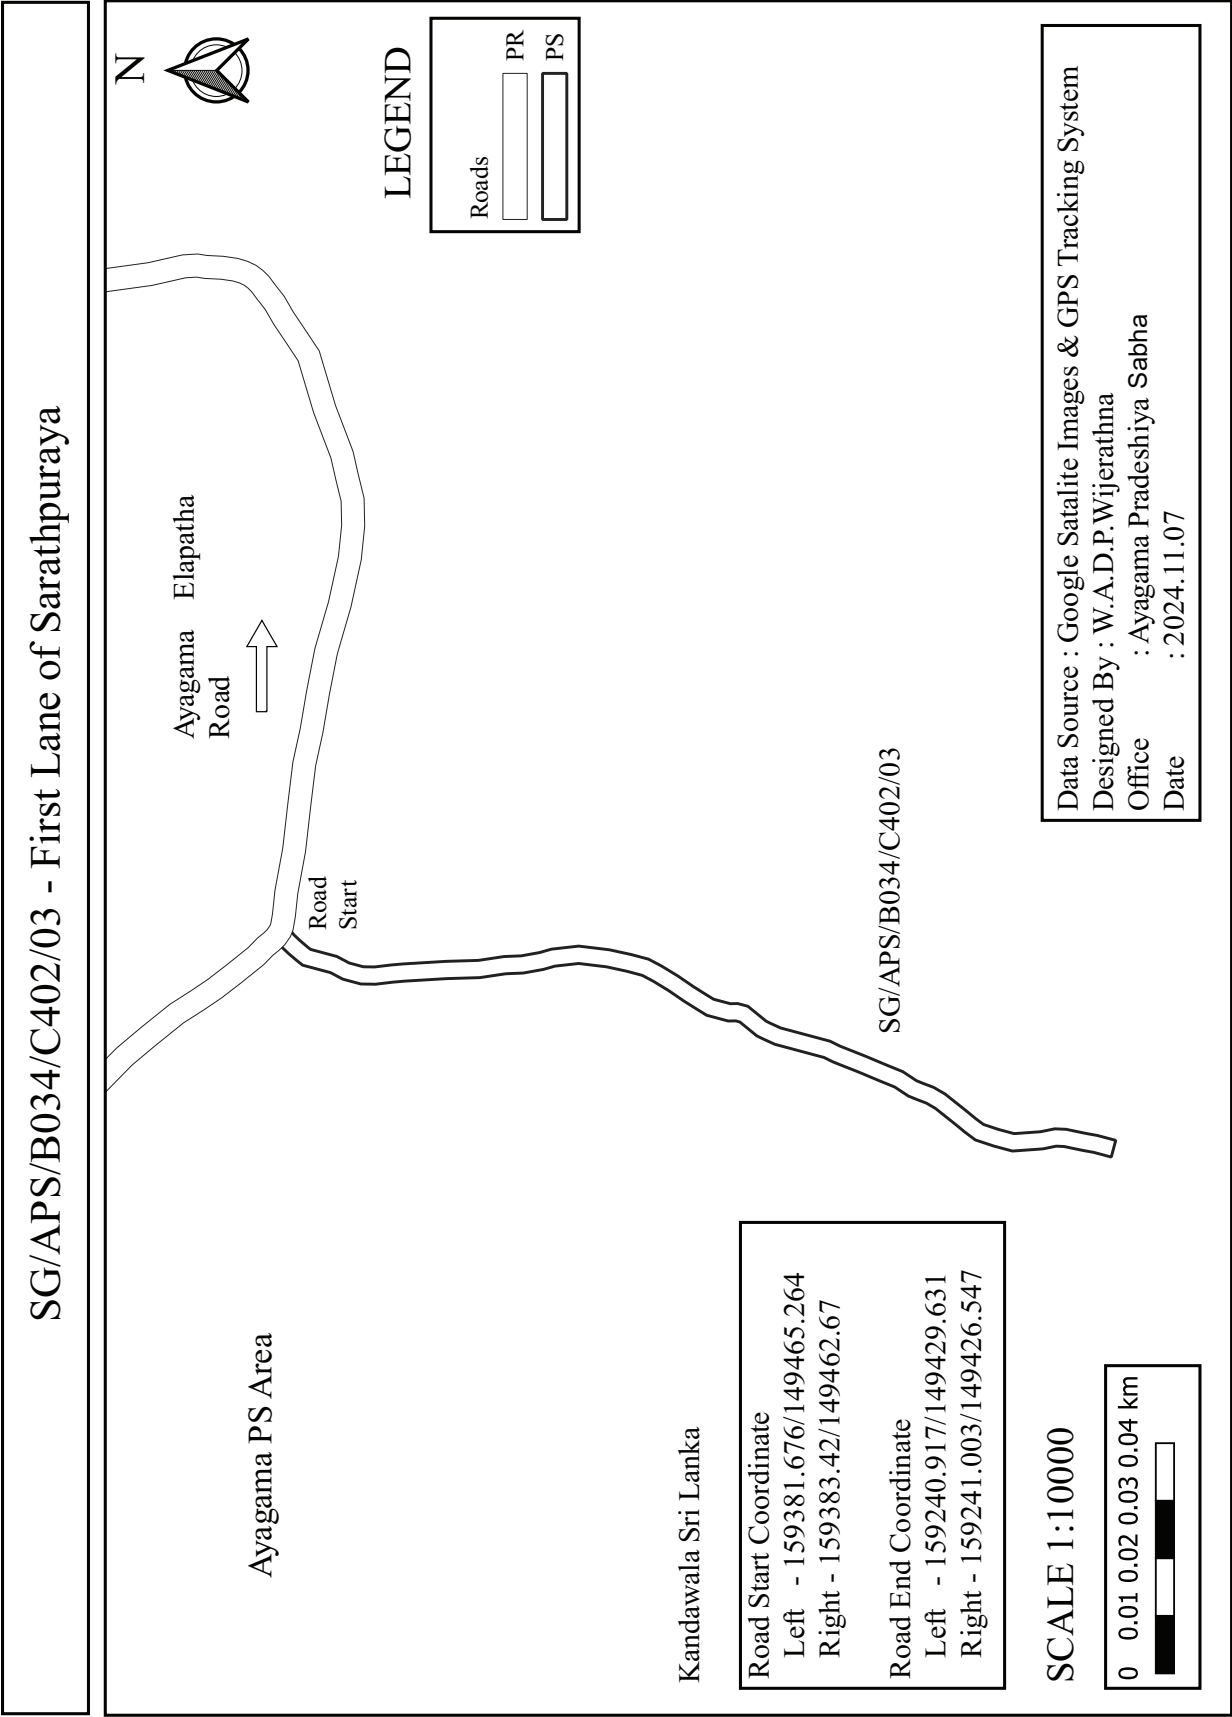


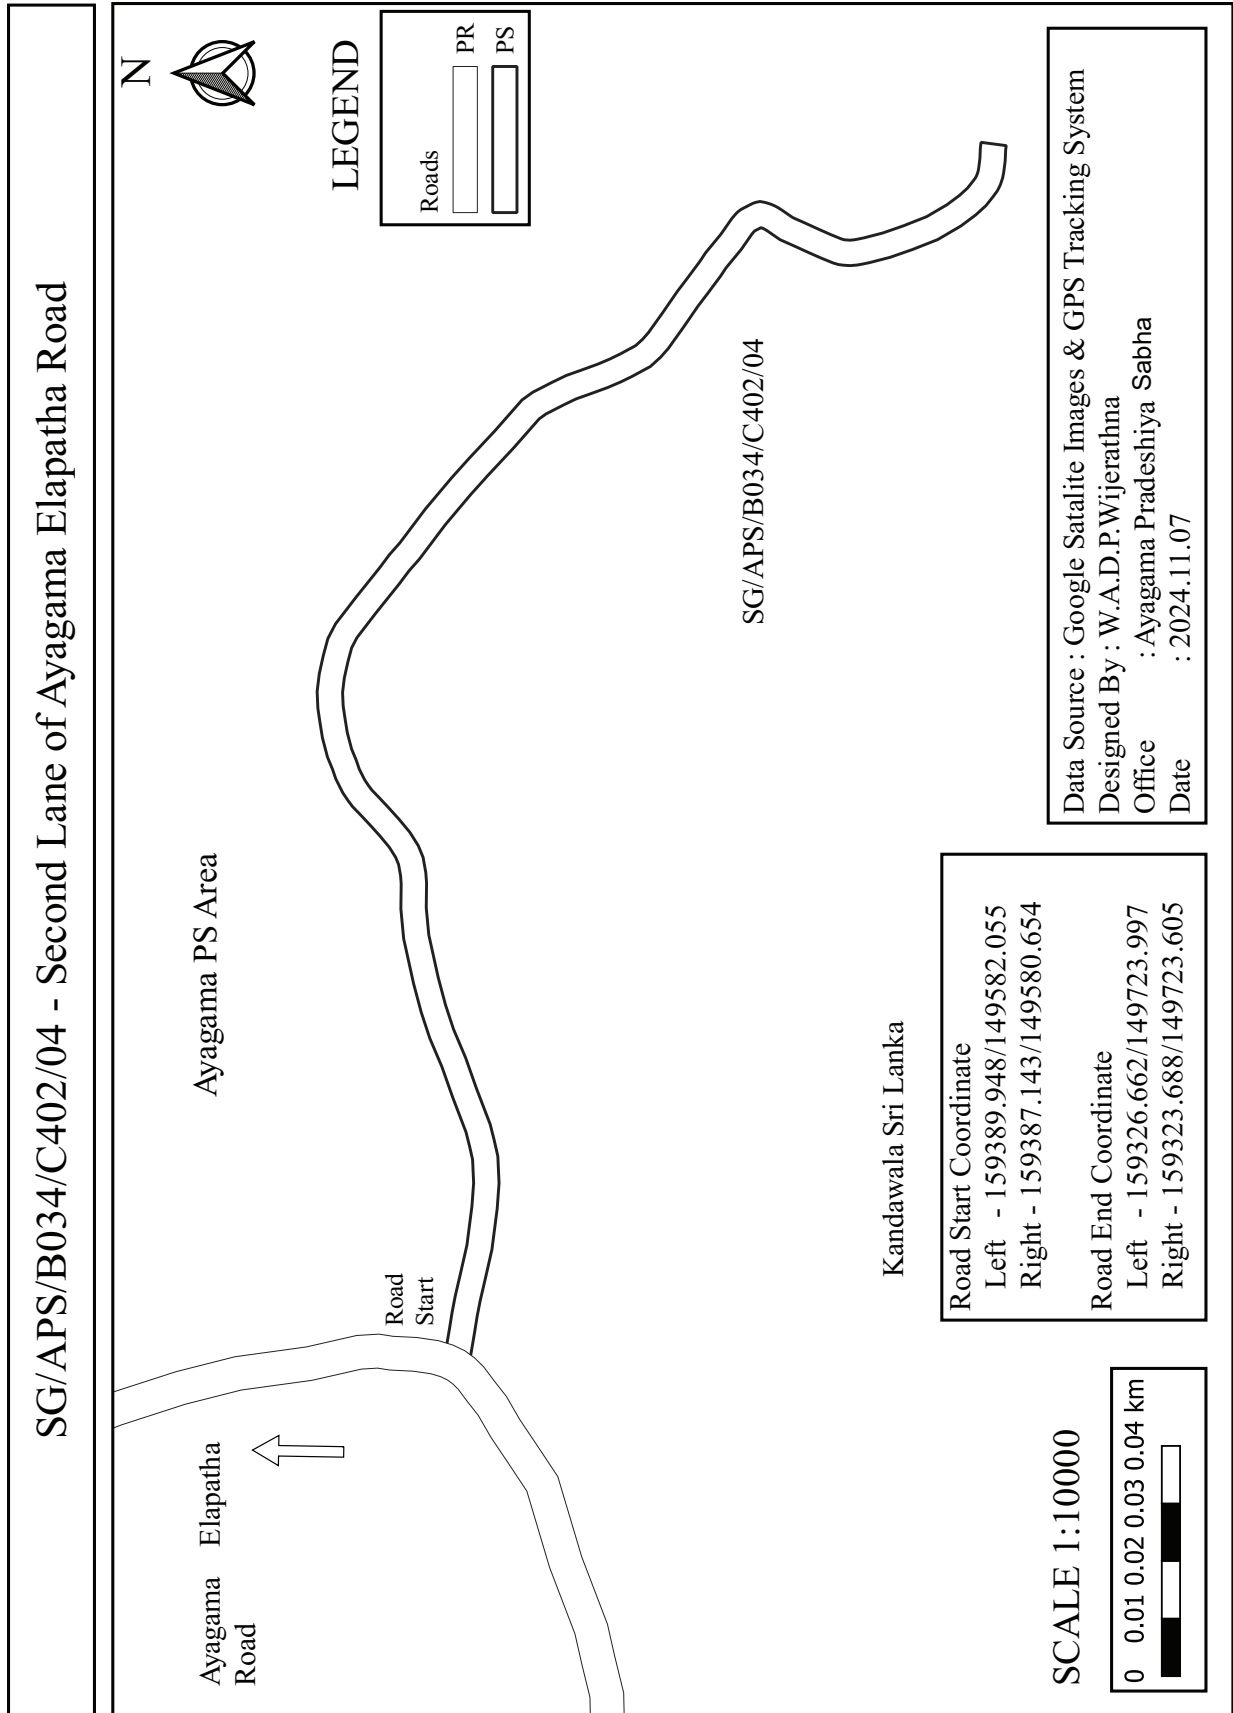


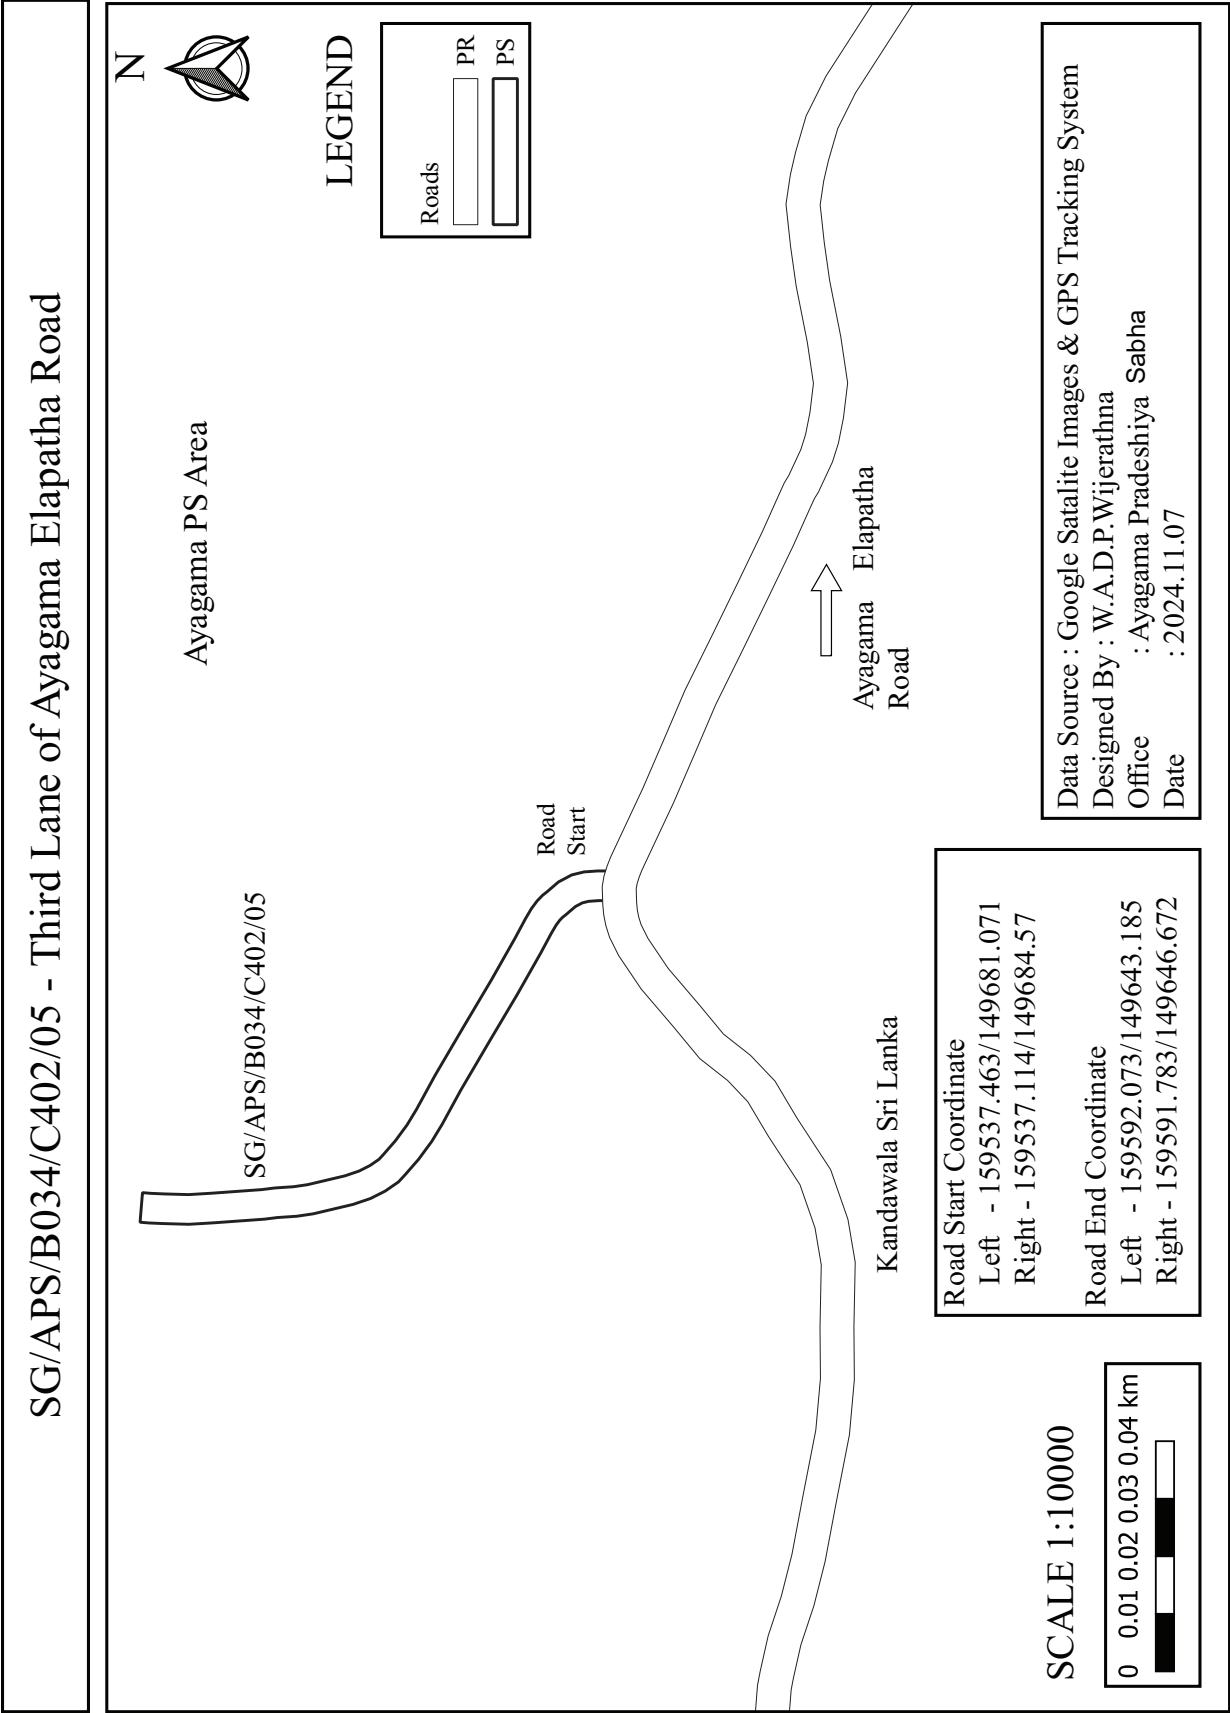


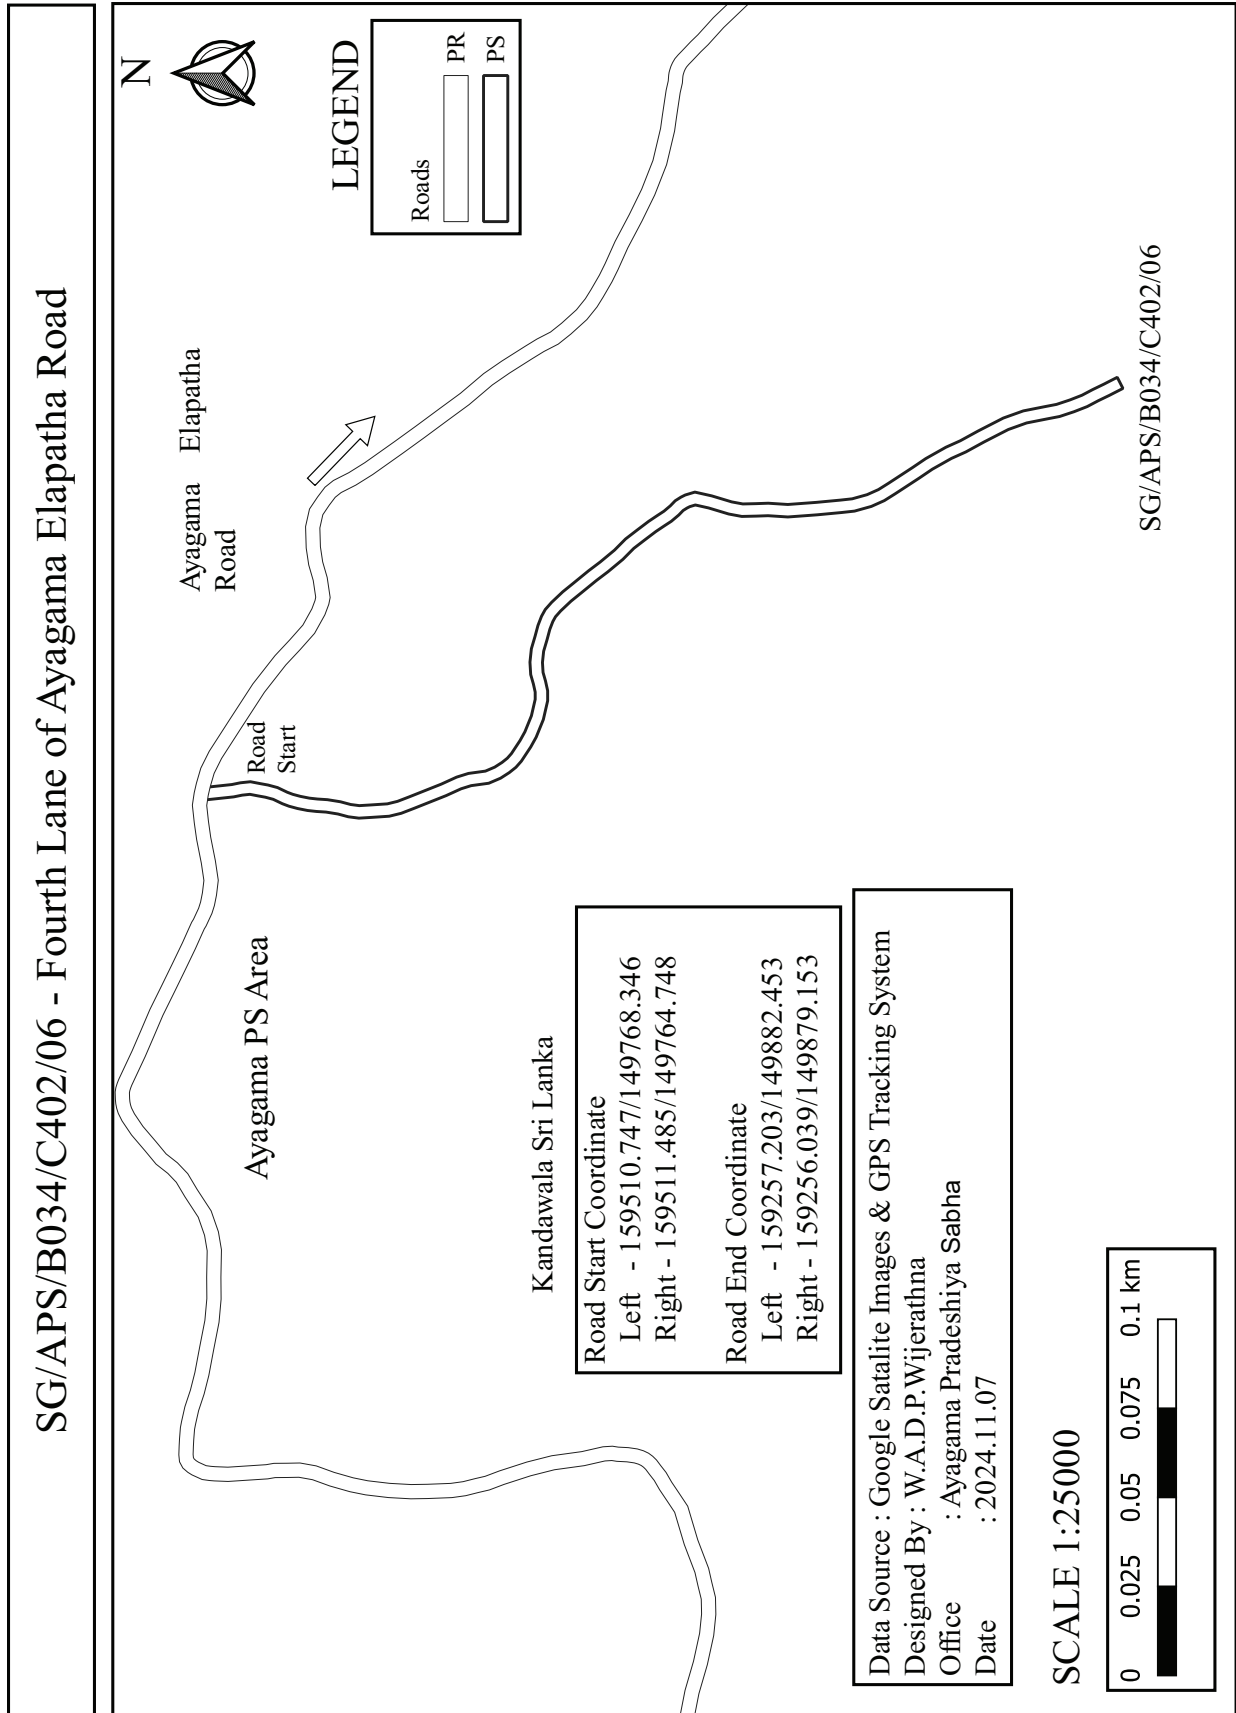


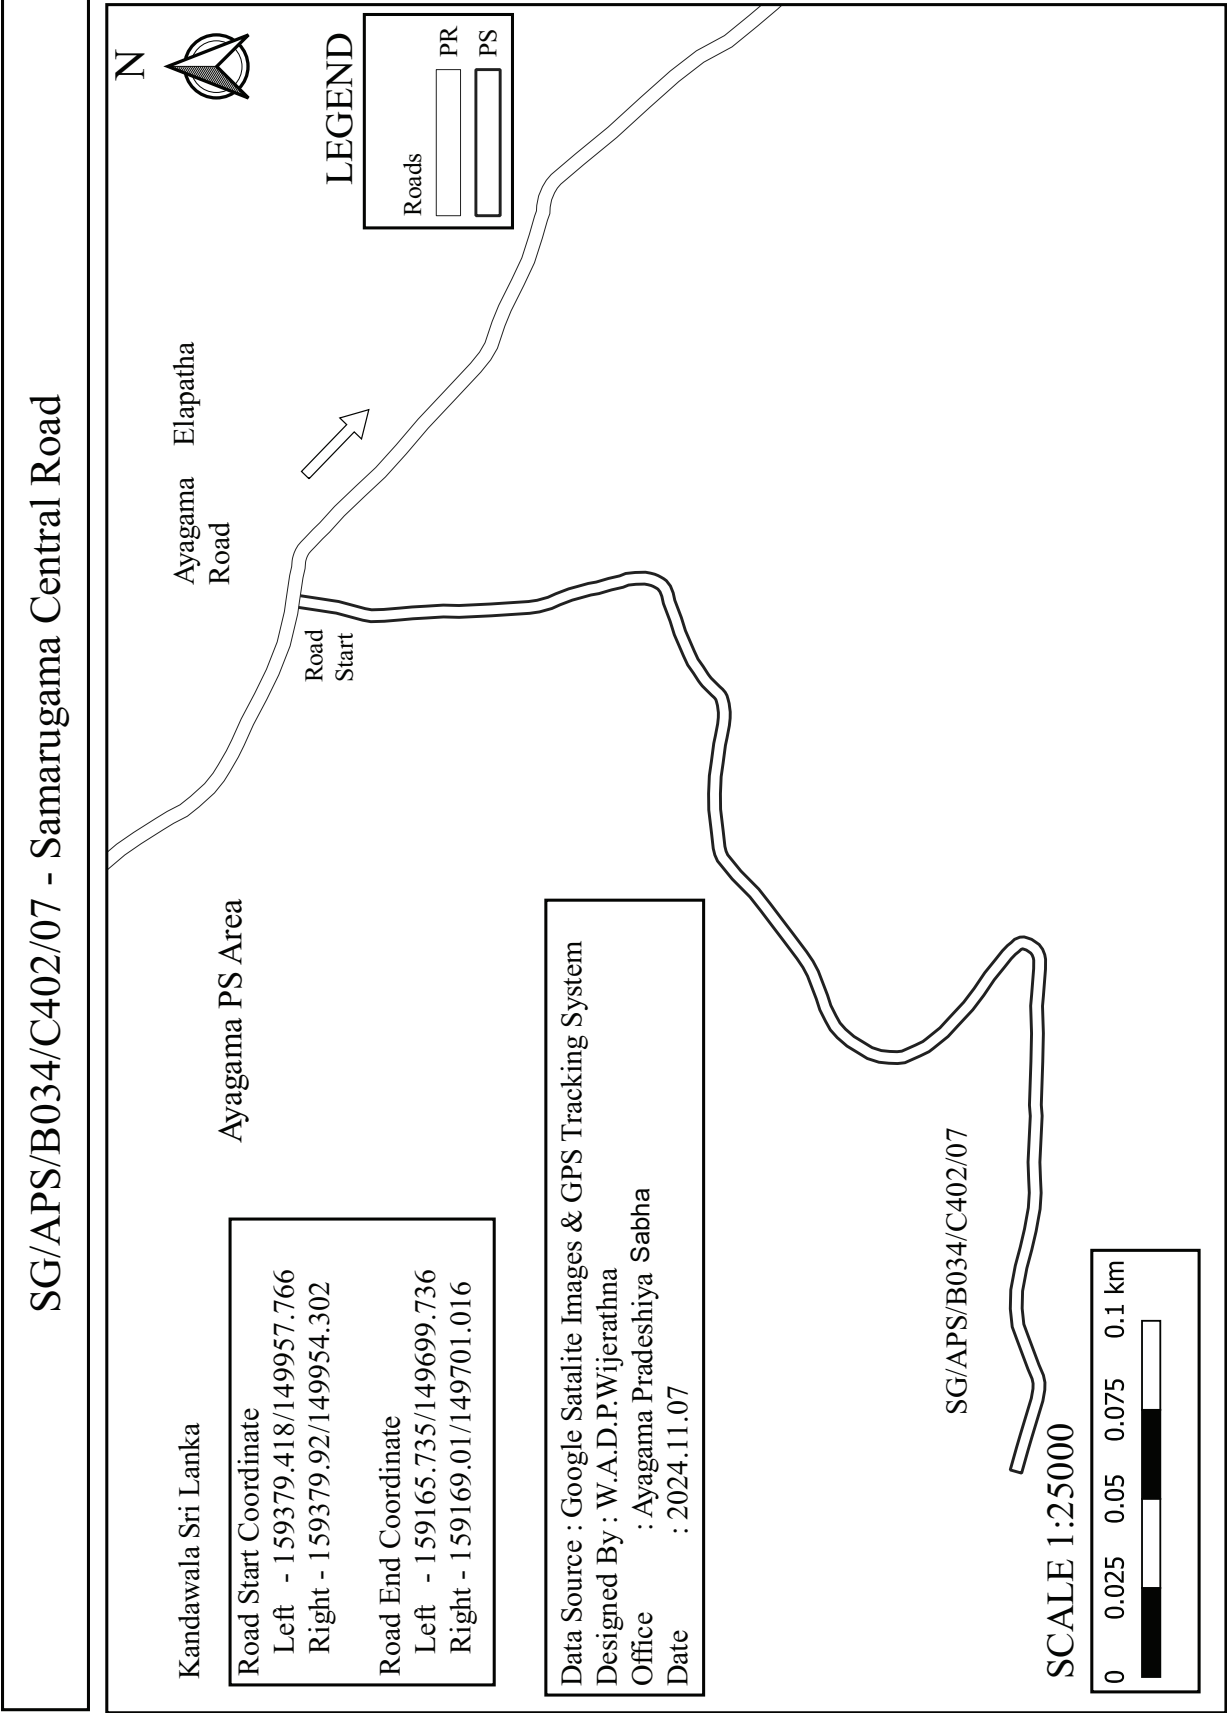


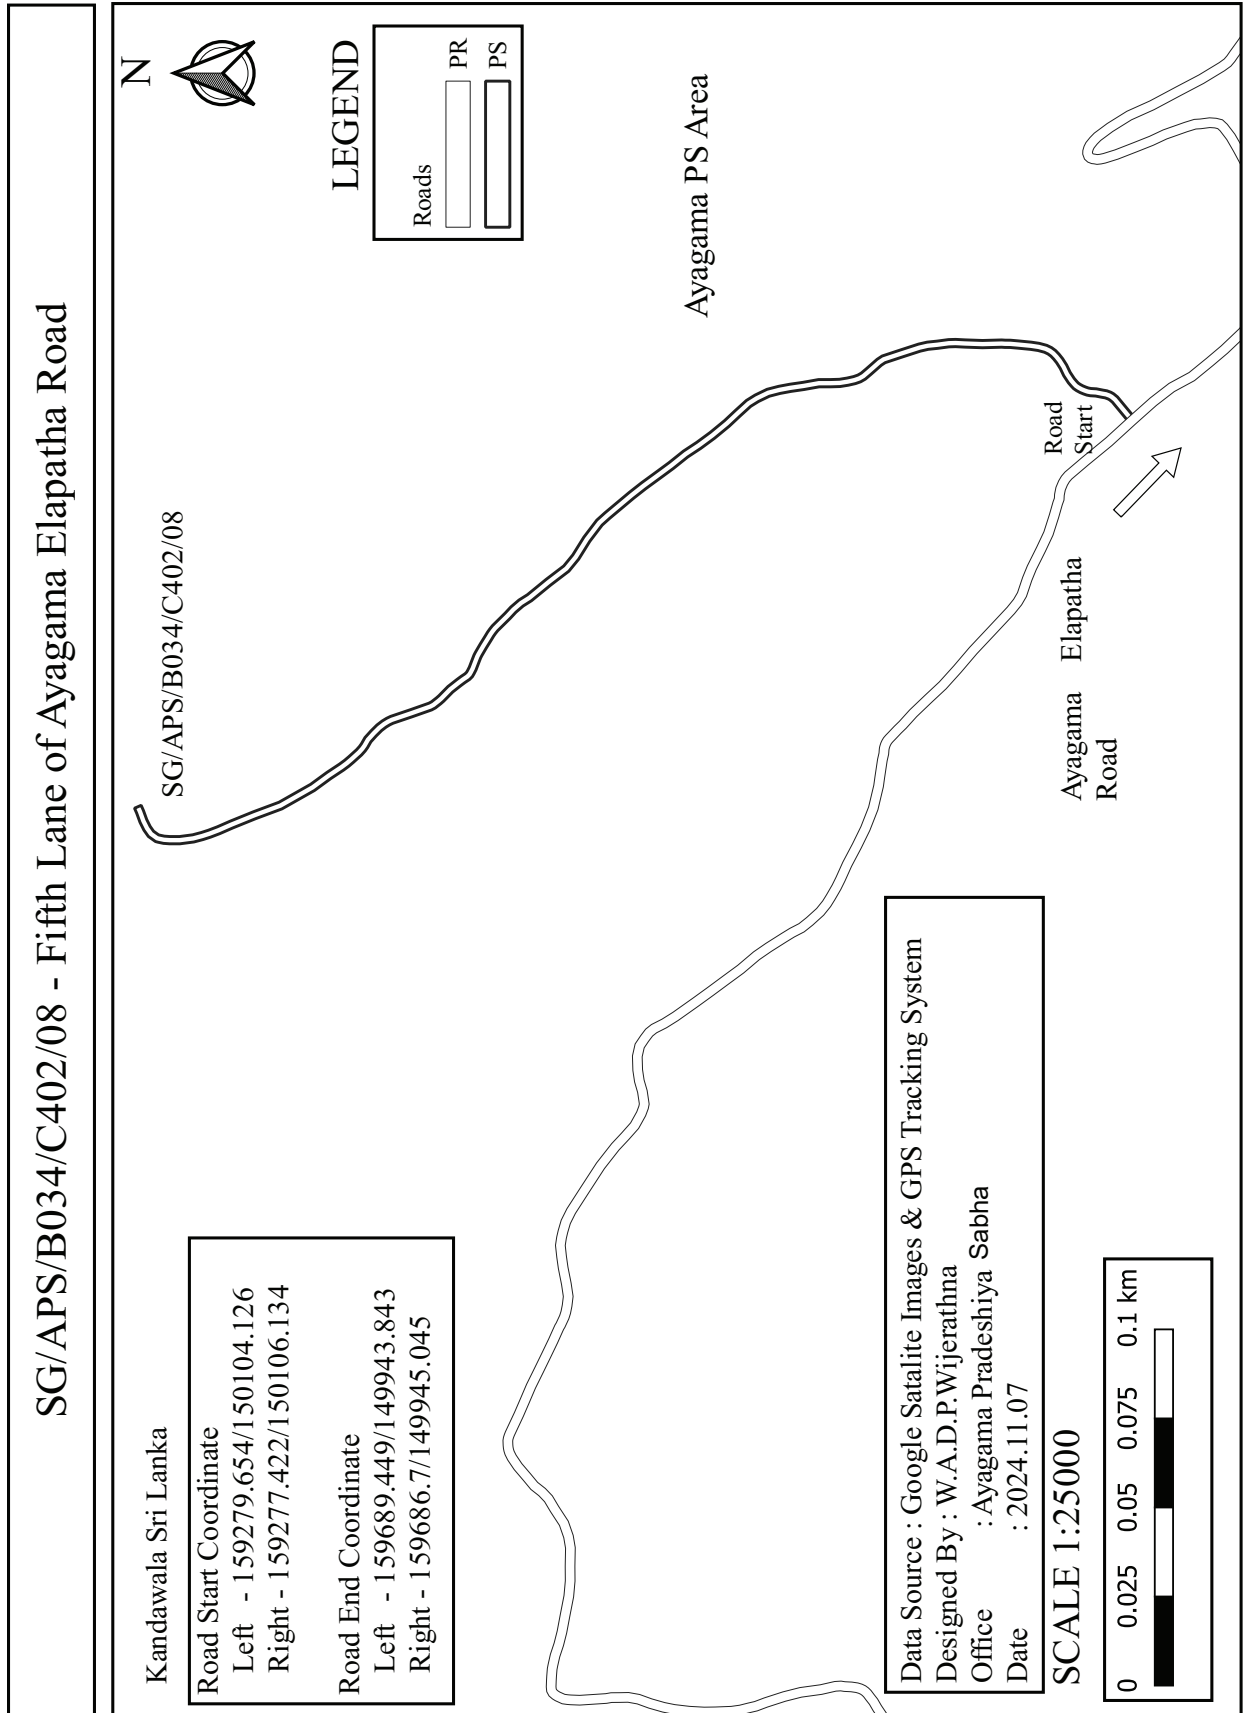


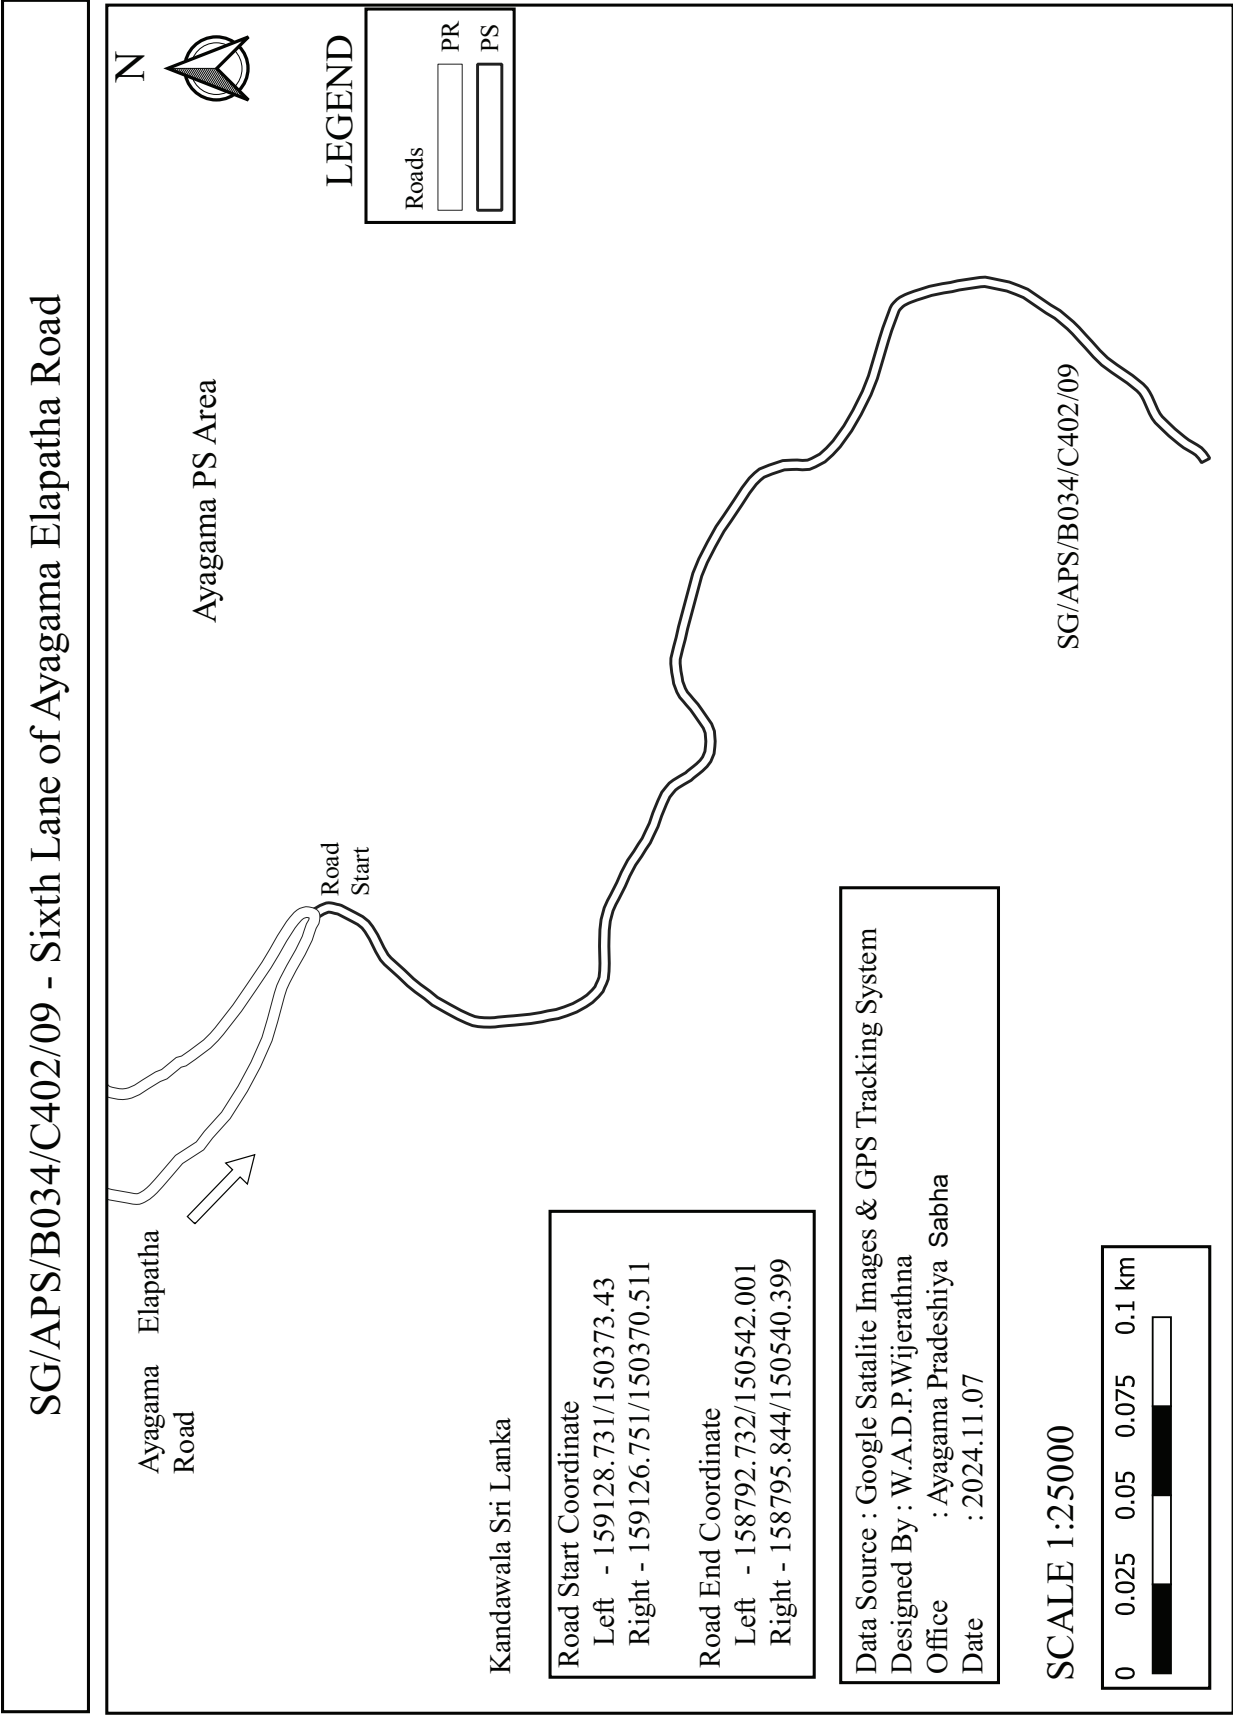

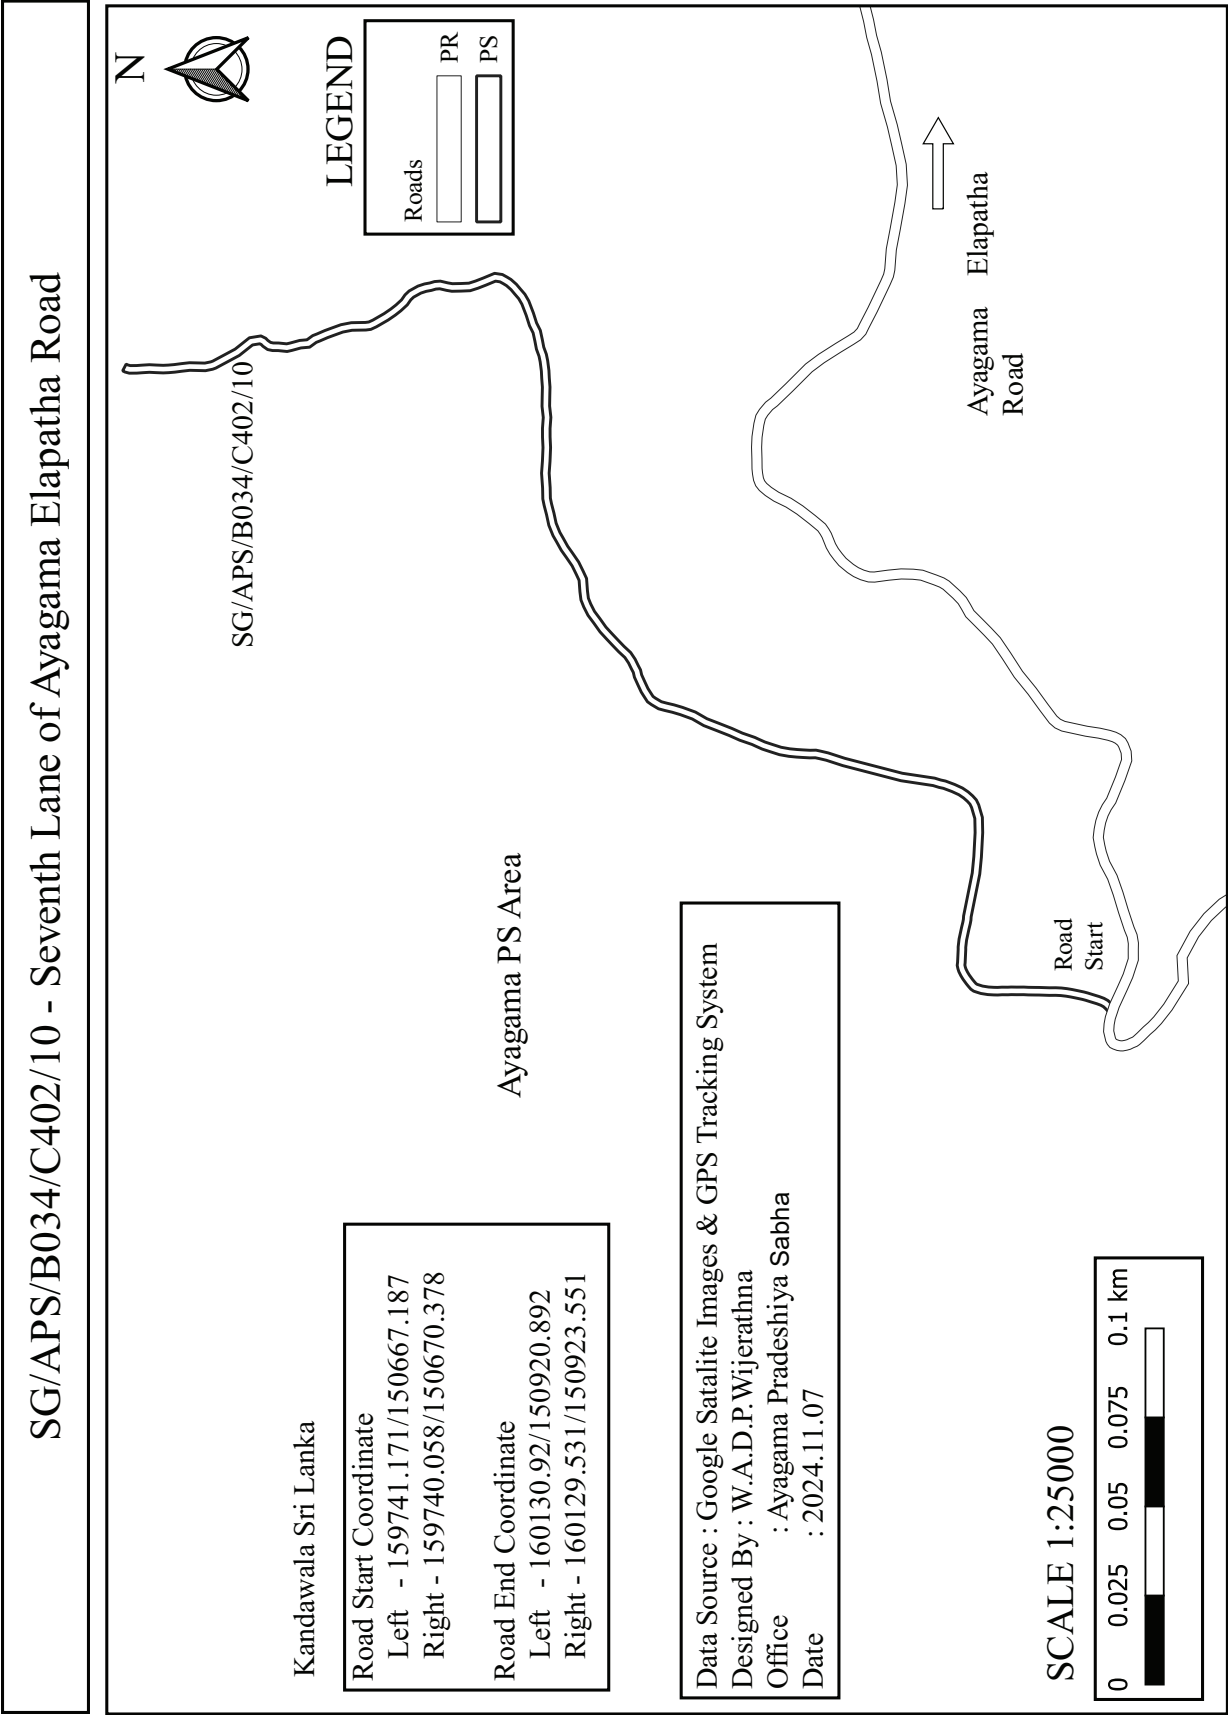


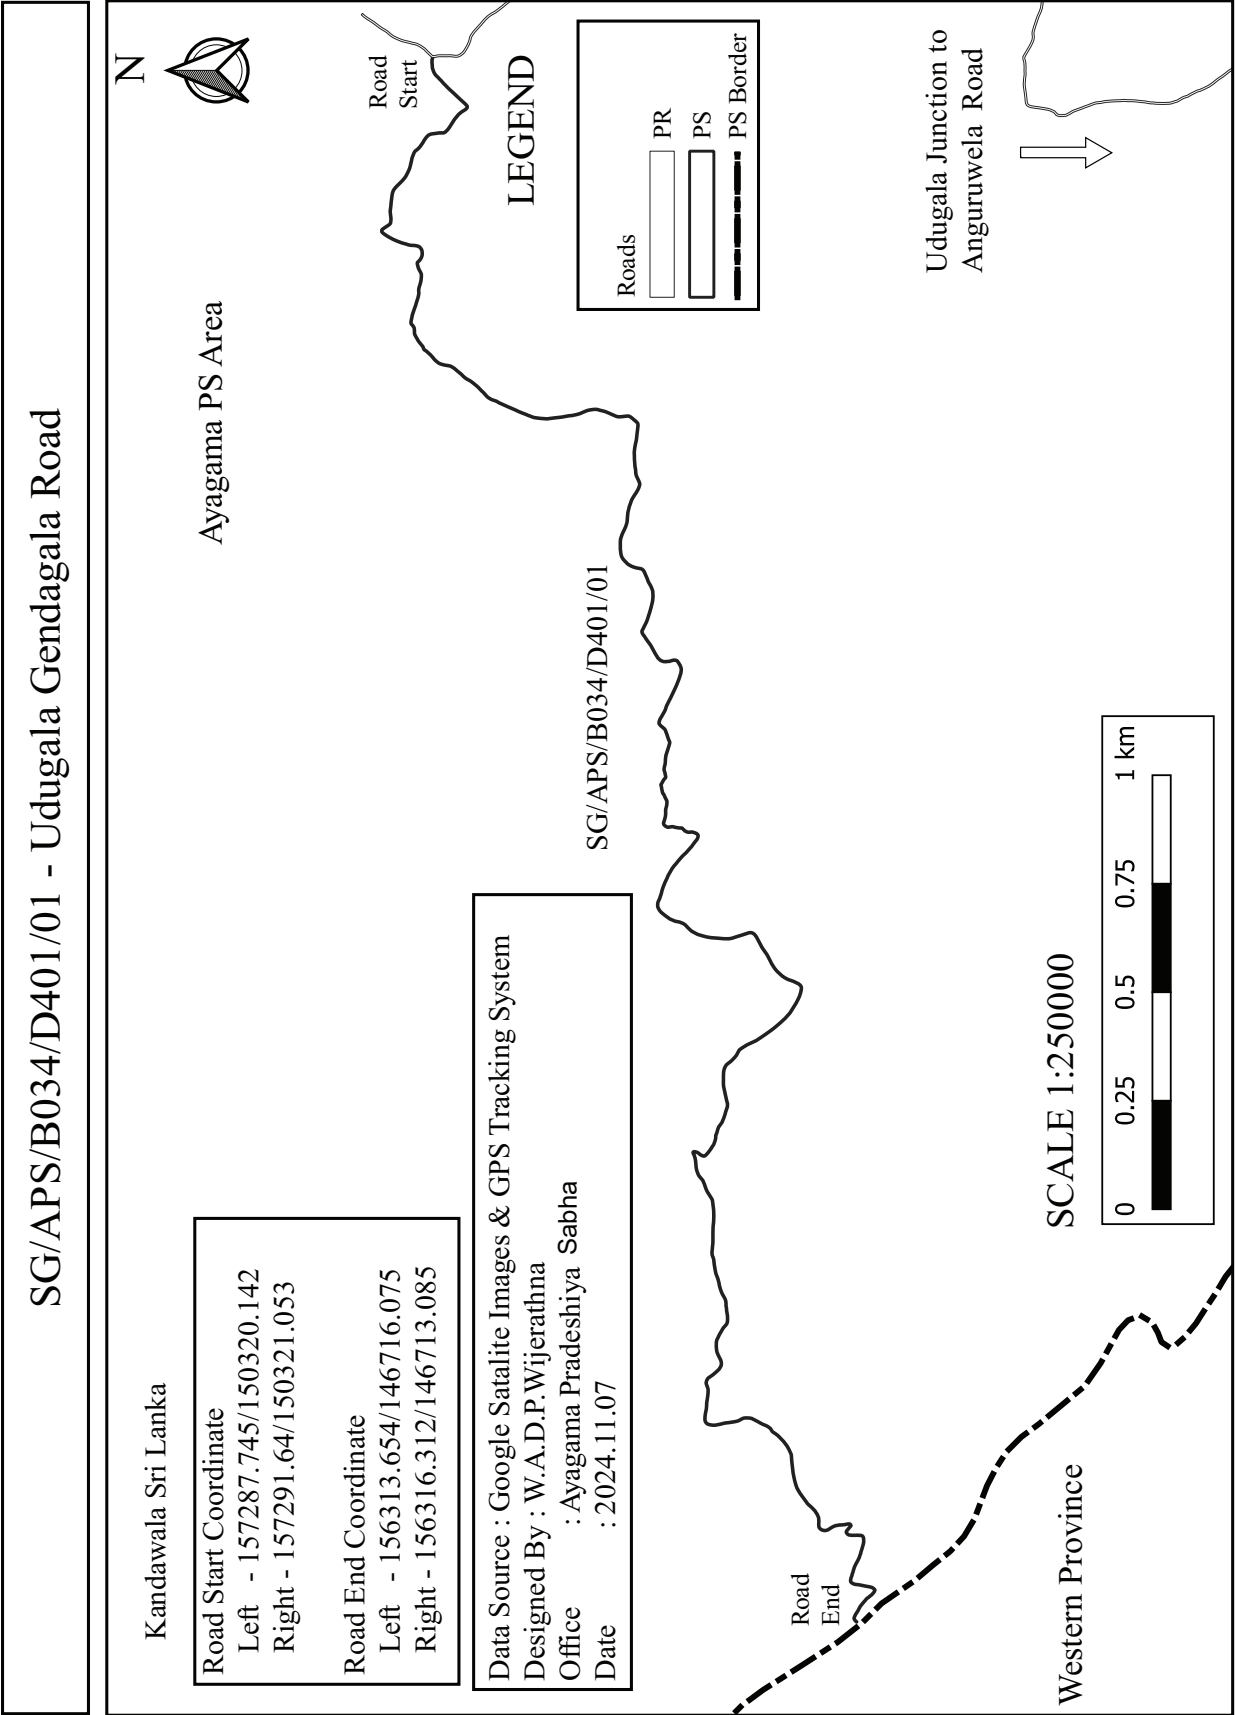


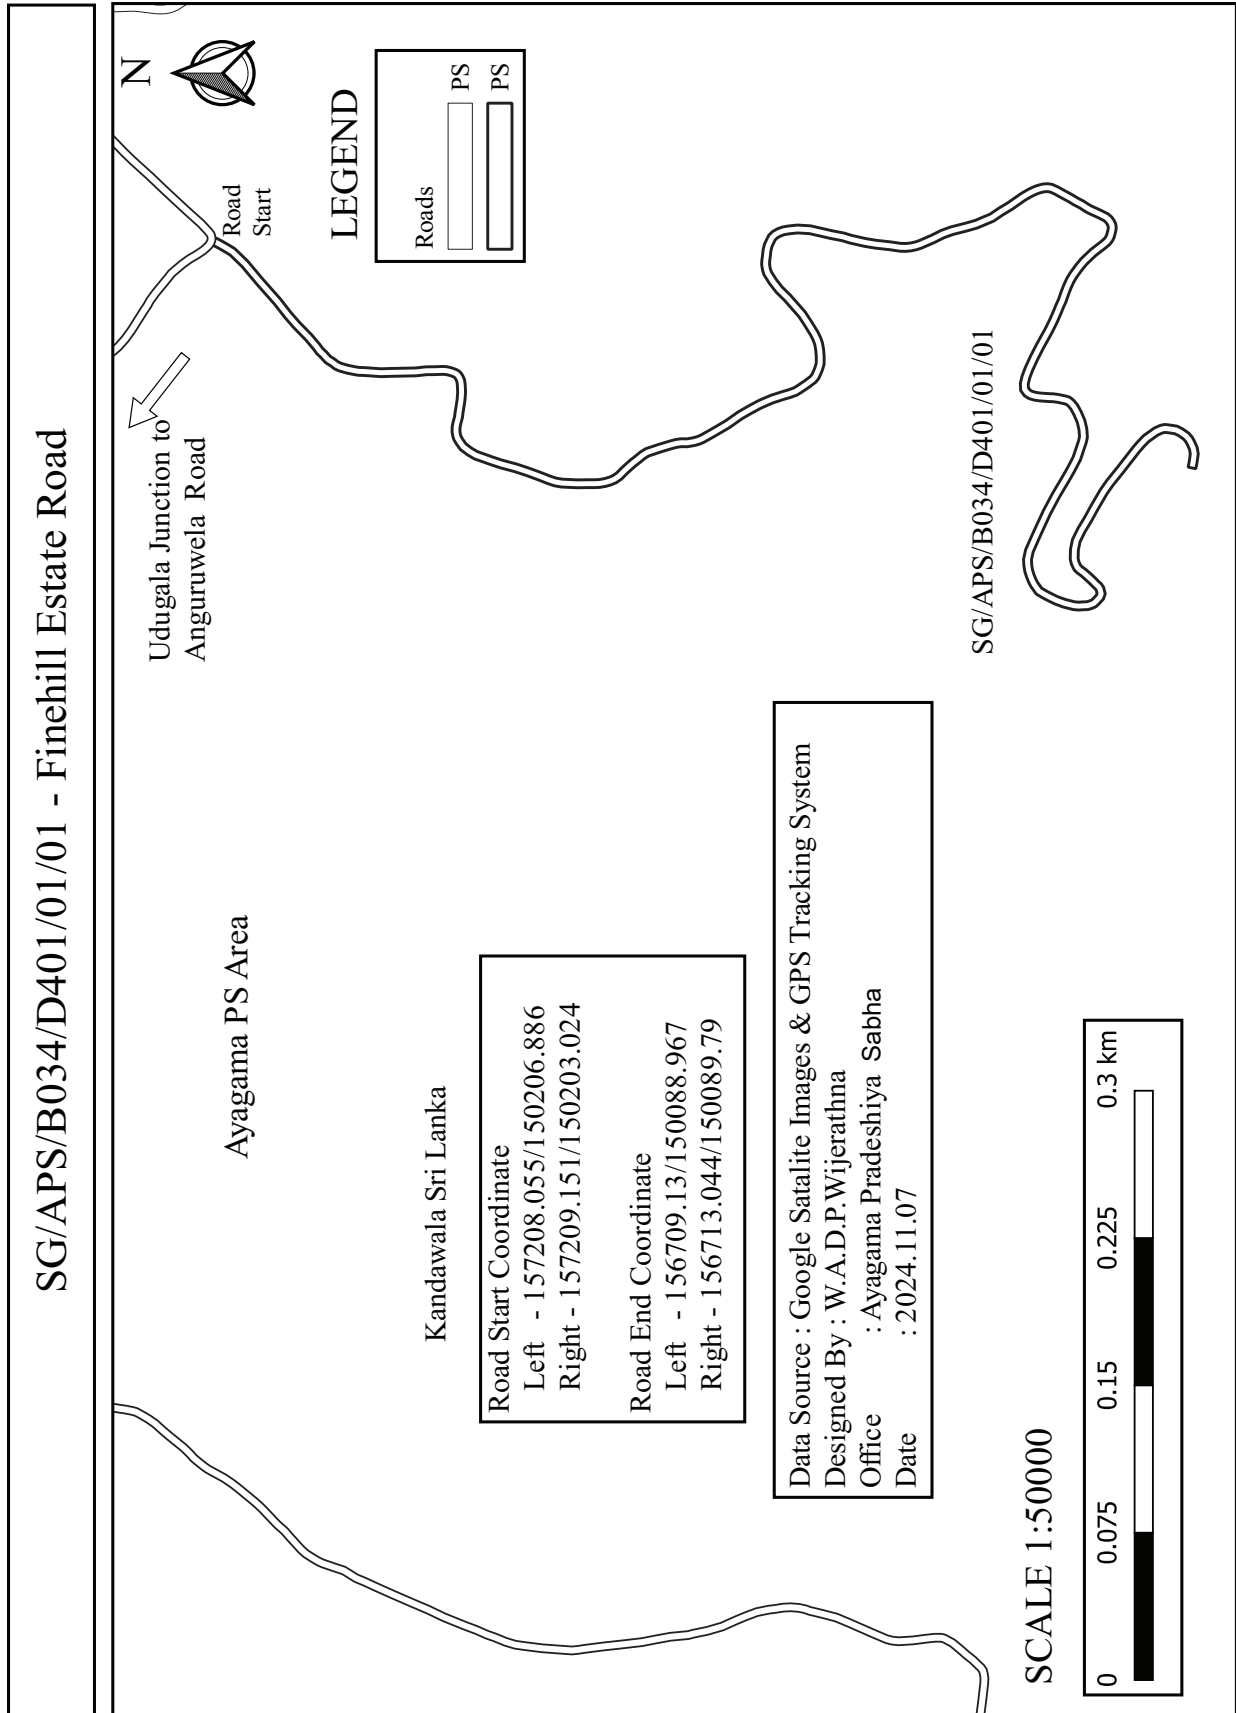

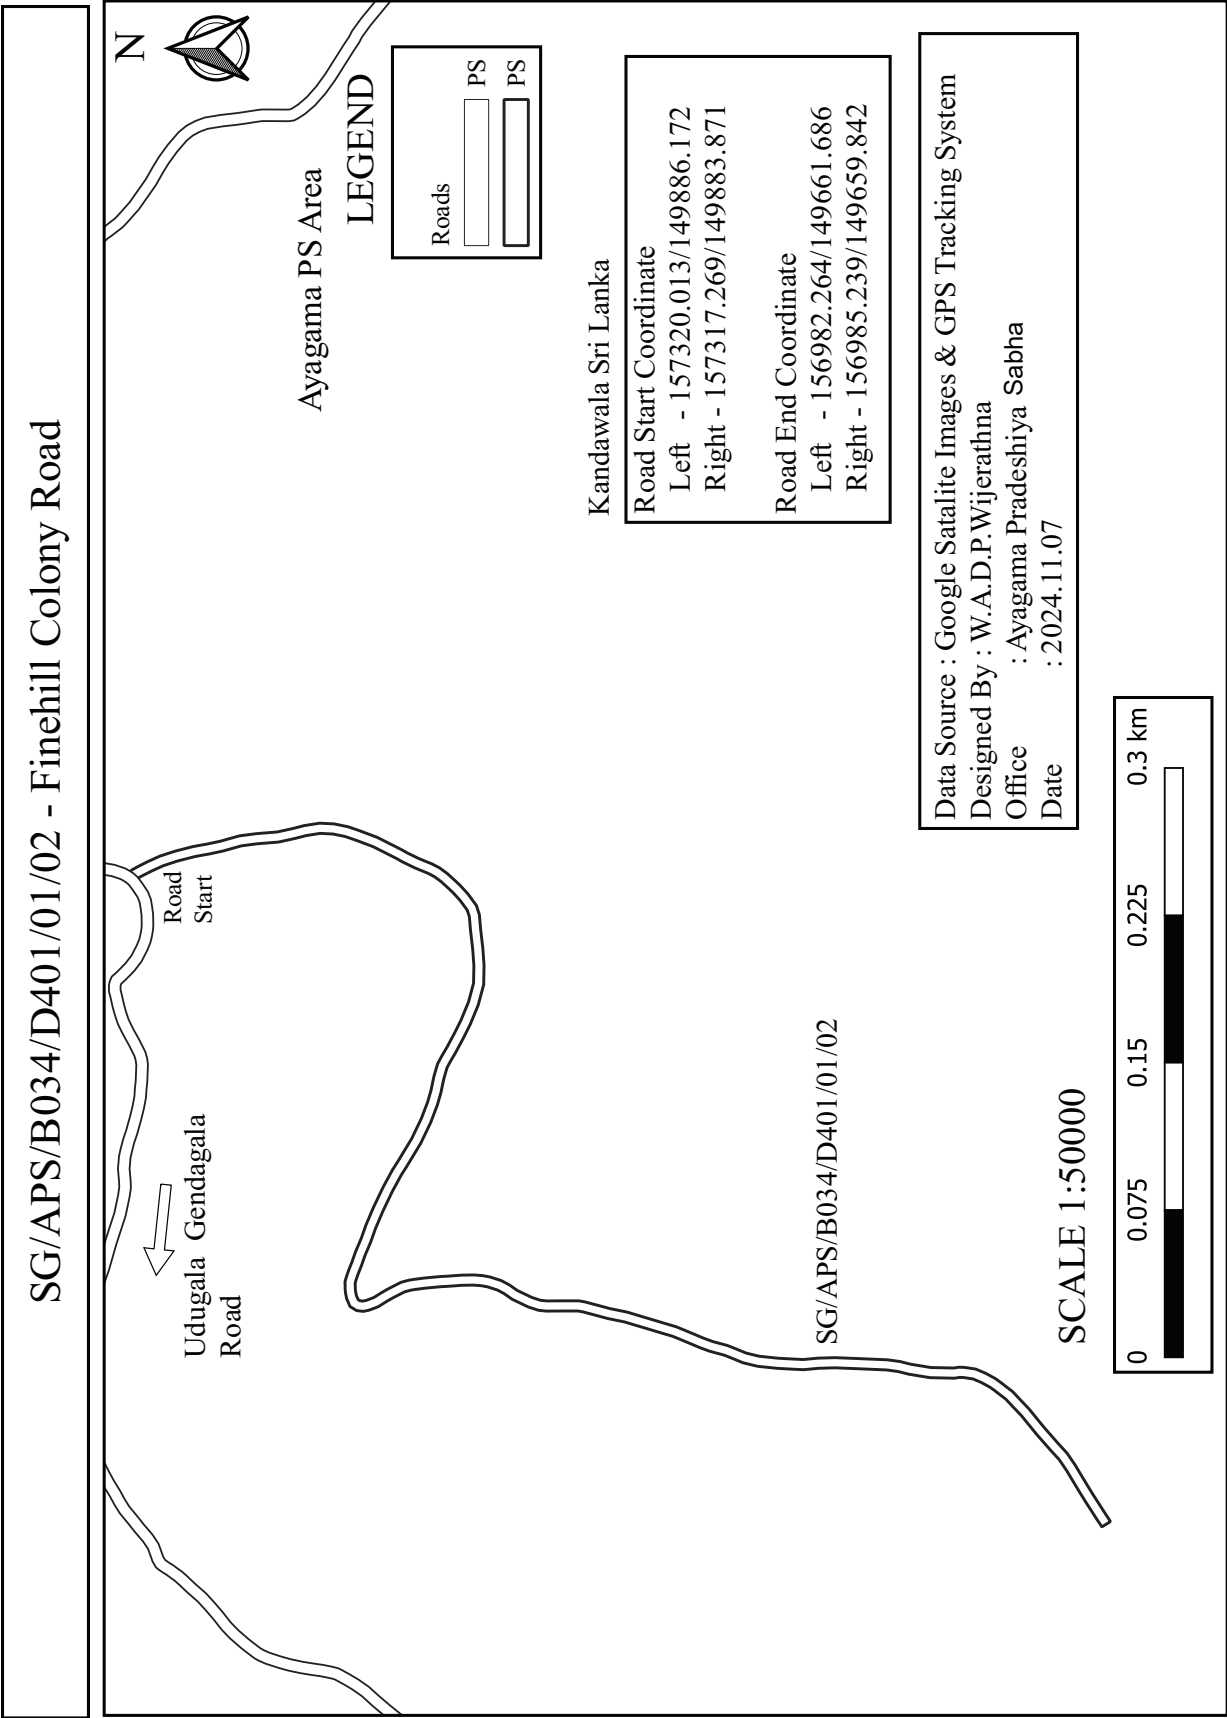



SG/APS/B034/D401/01/02/01 - Finehill Ihala Road

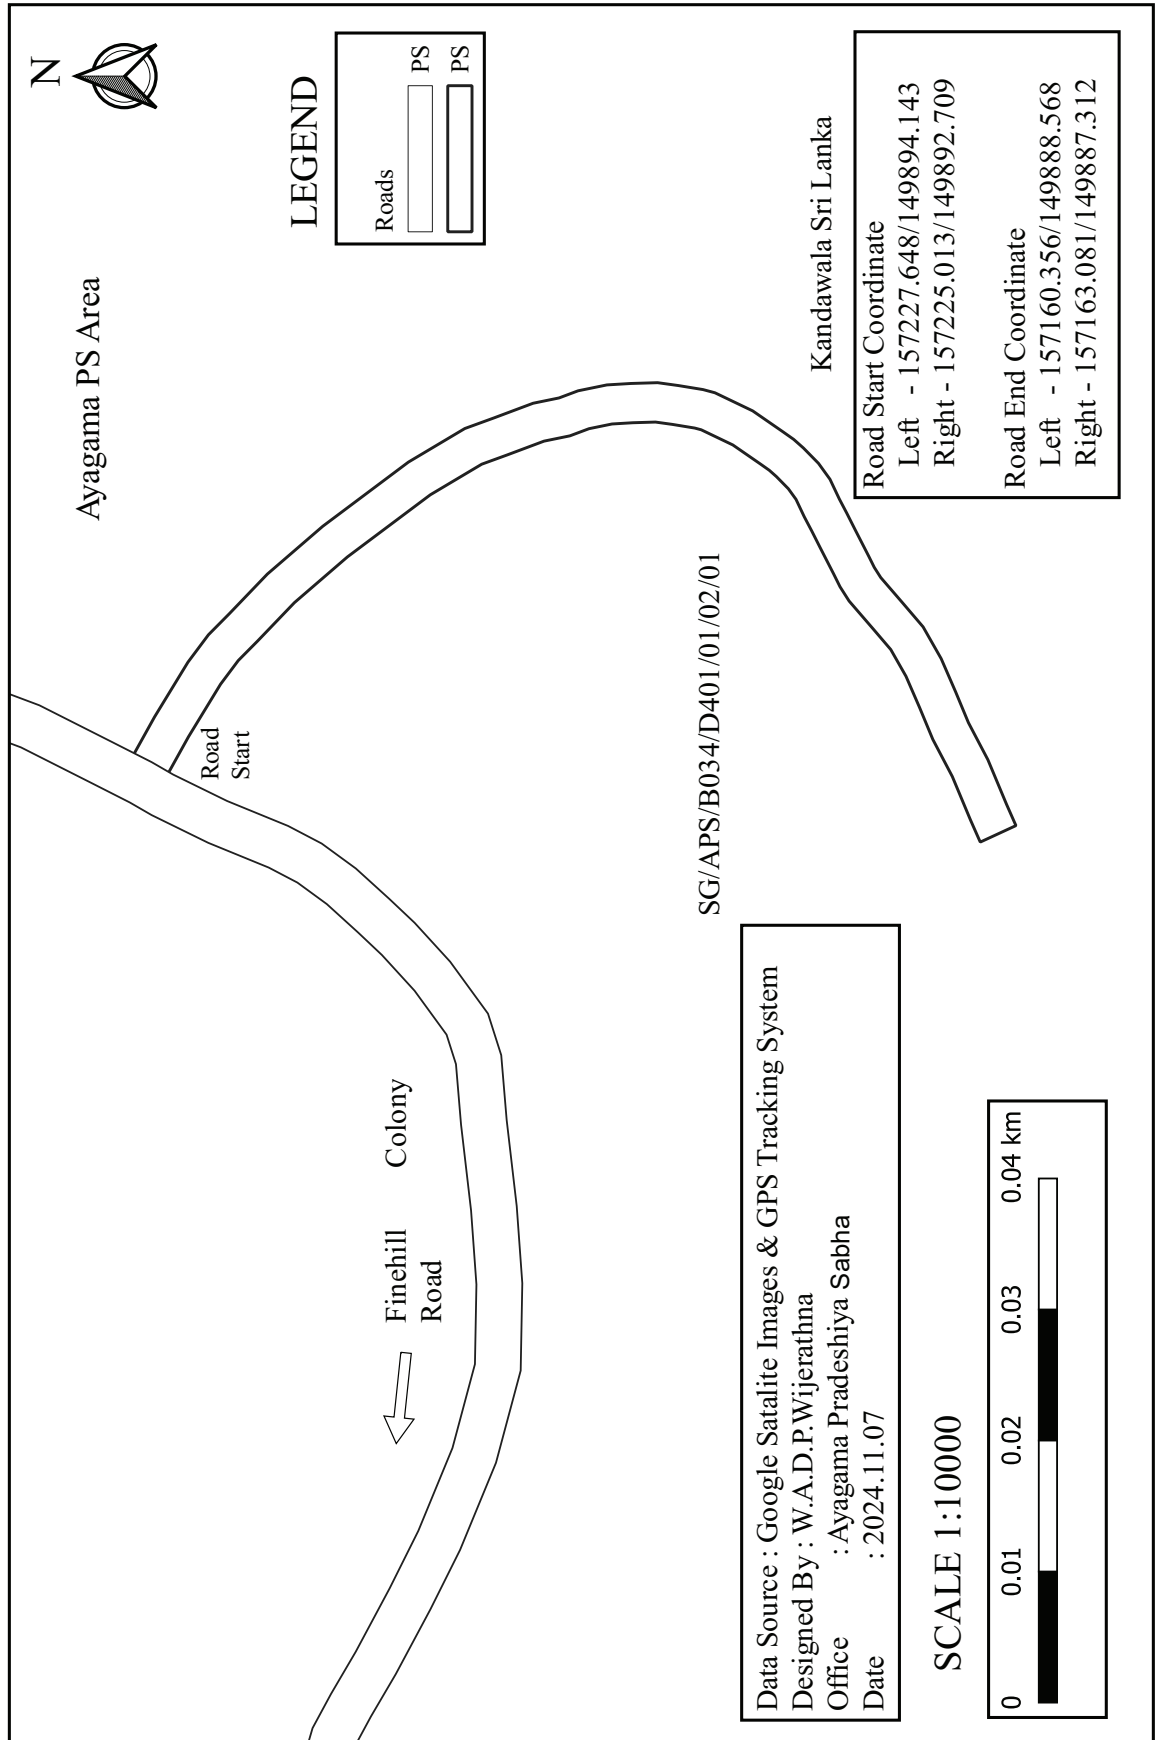


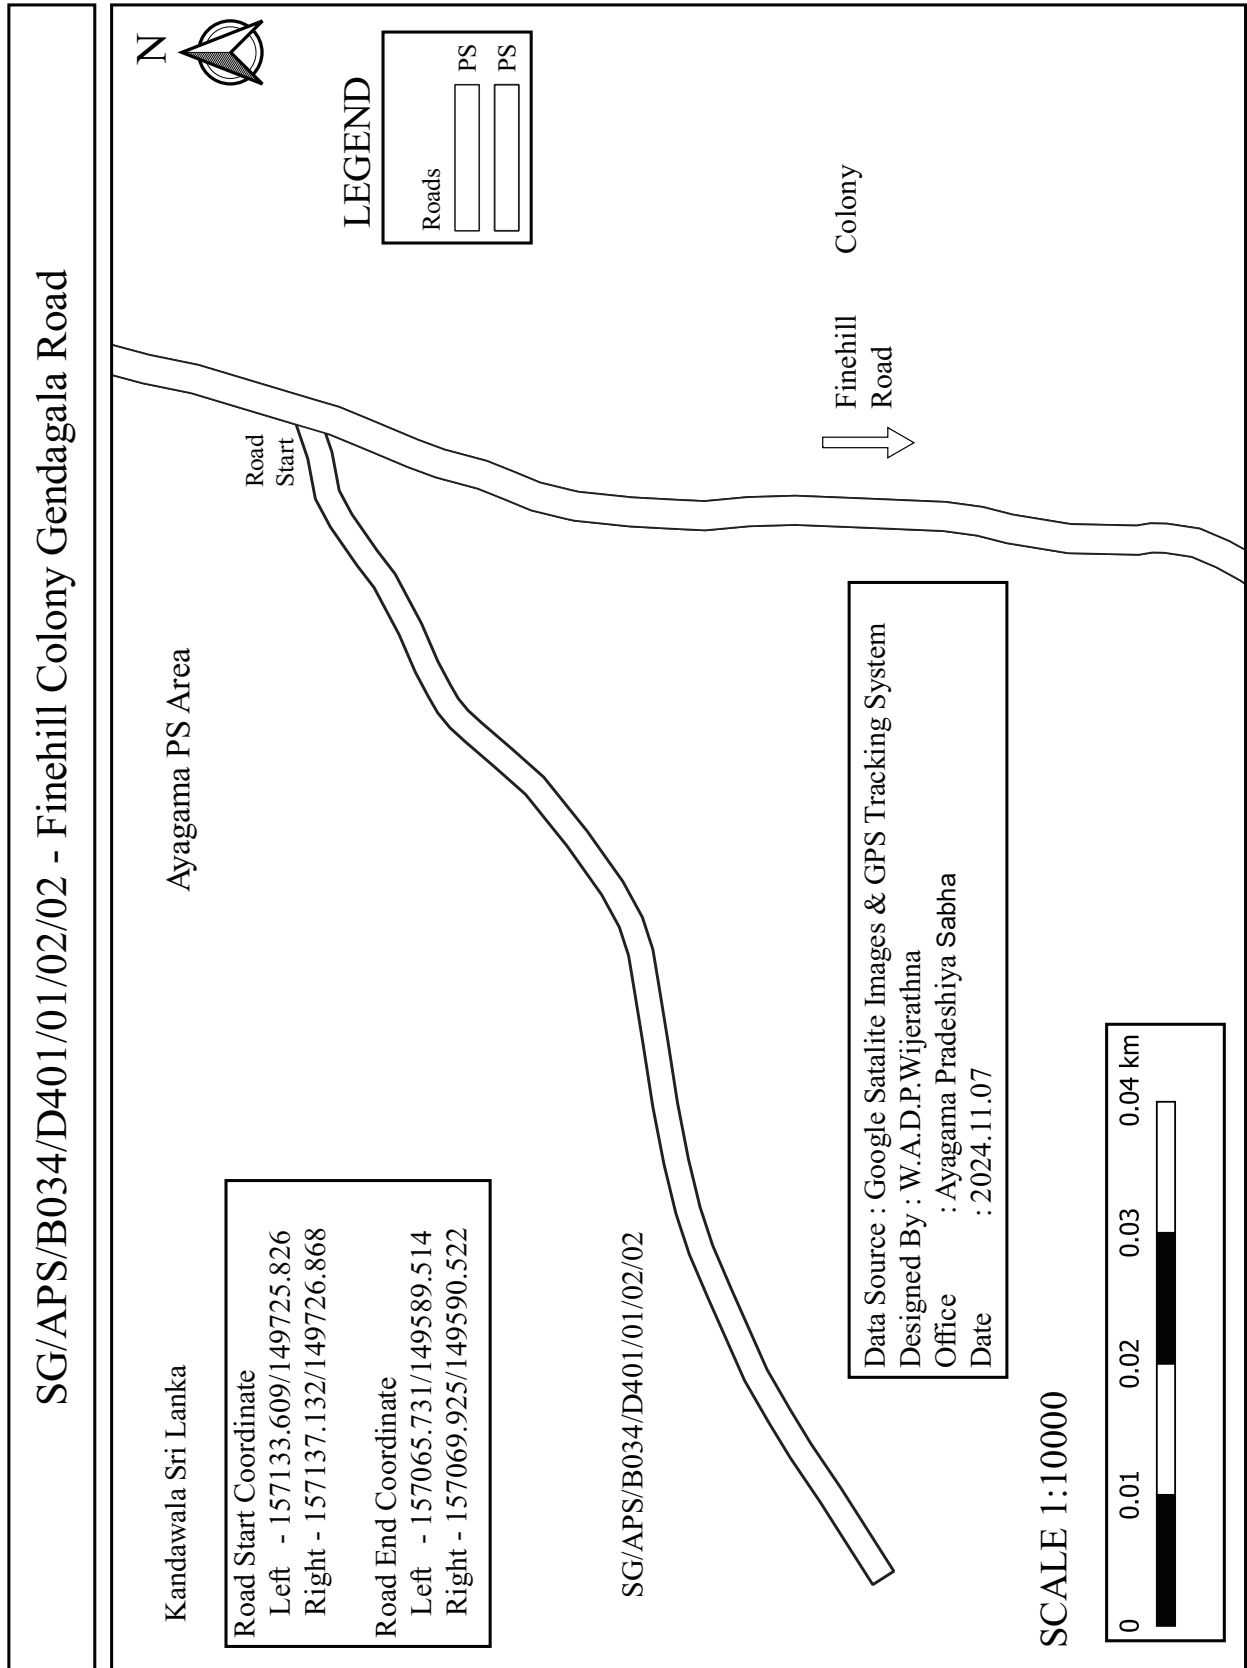


SG/APS/B034/D401/01/02/03 - First Lane of Finehill Colony Gendagala Road

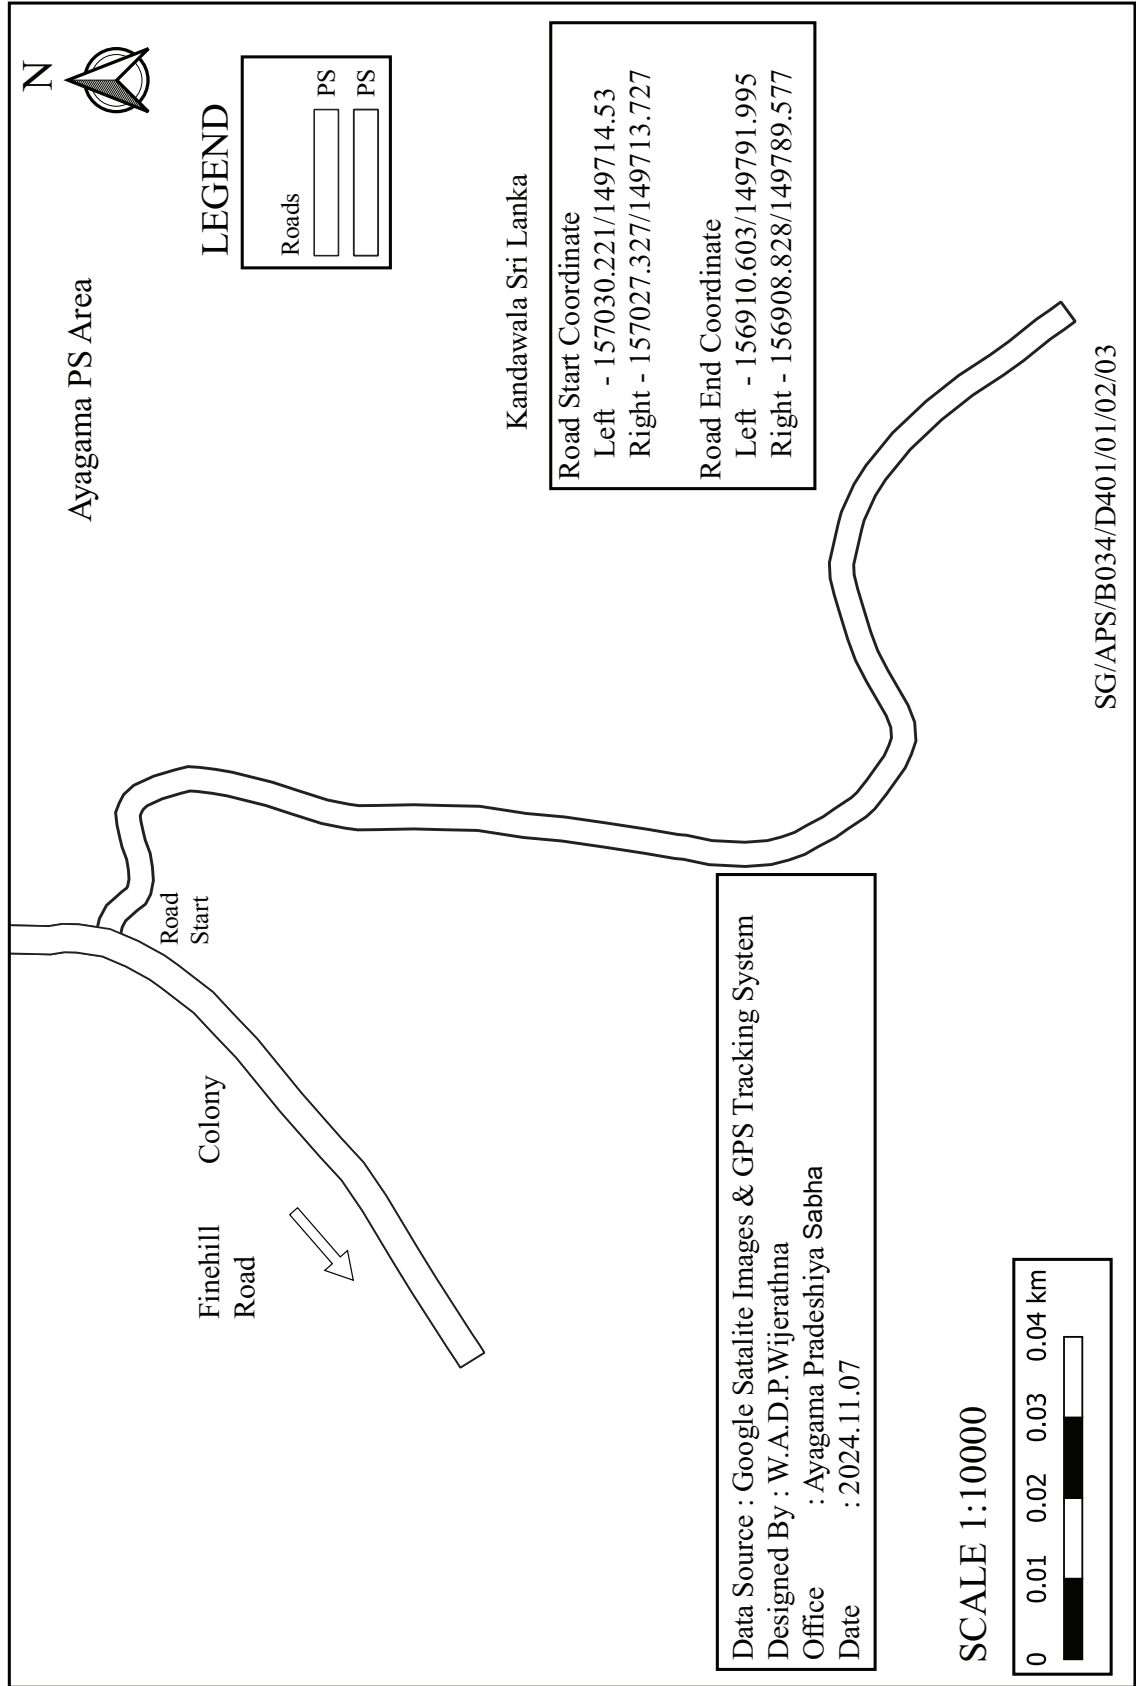


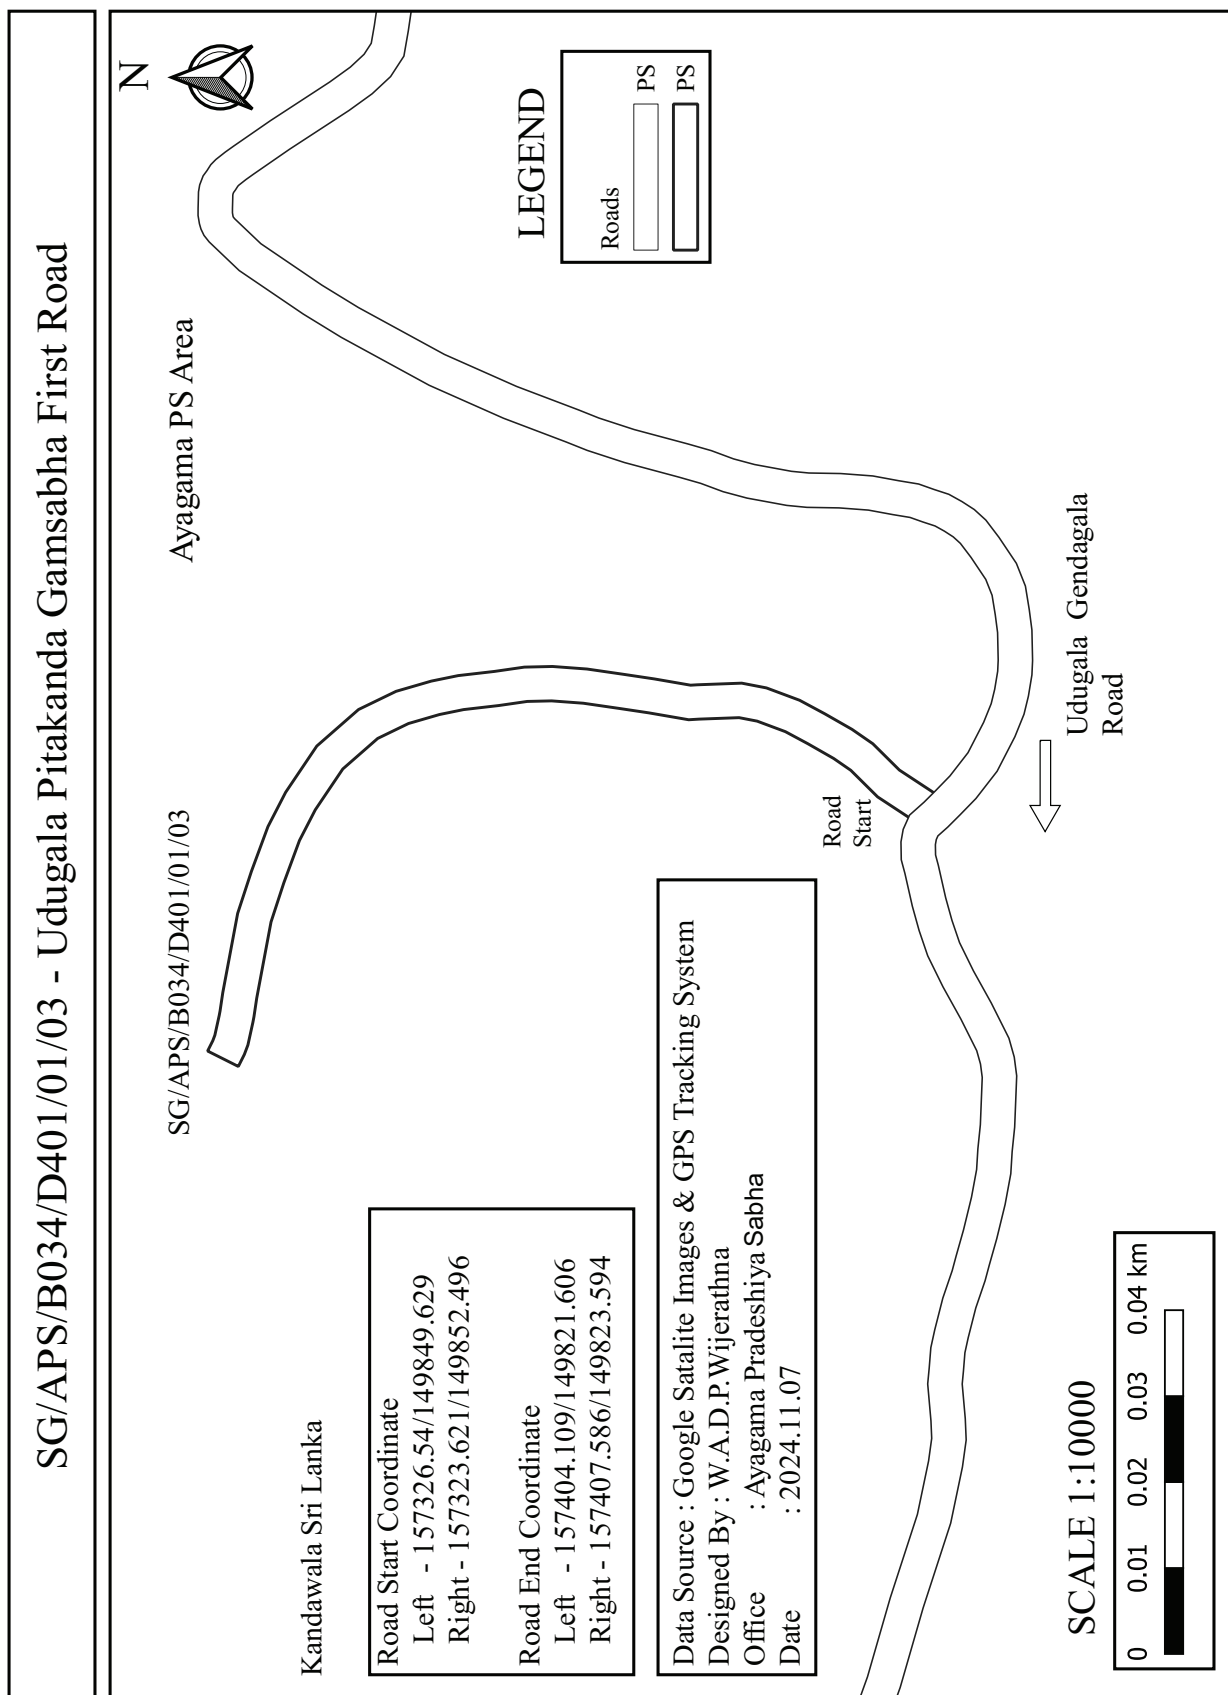


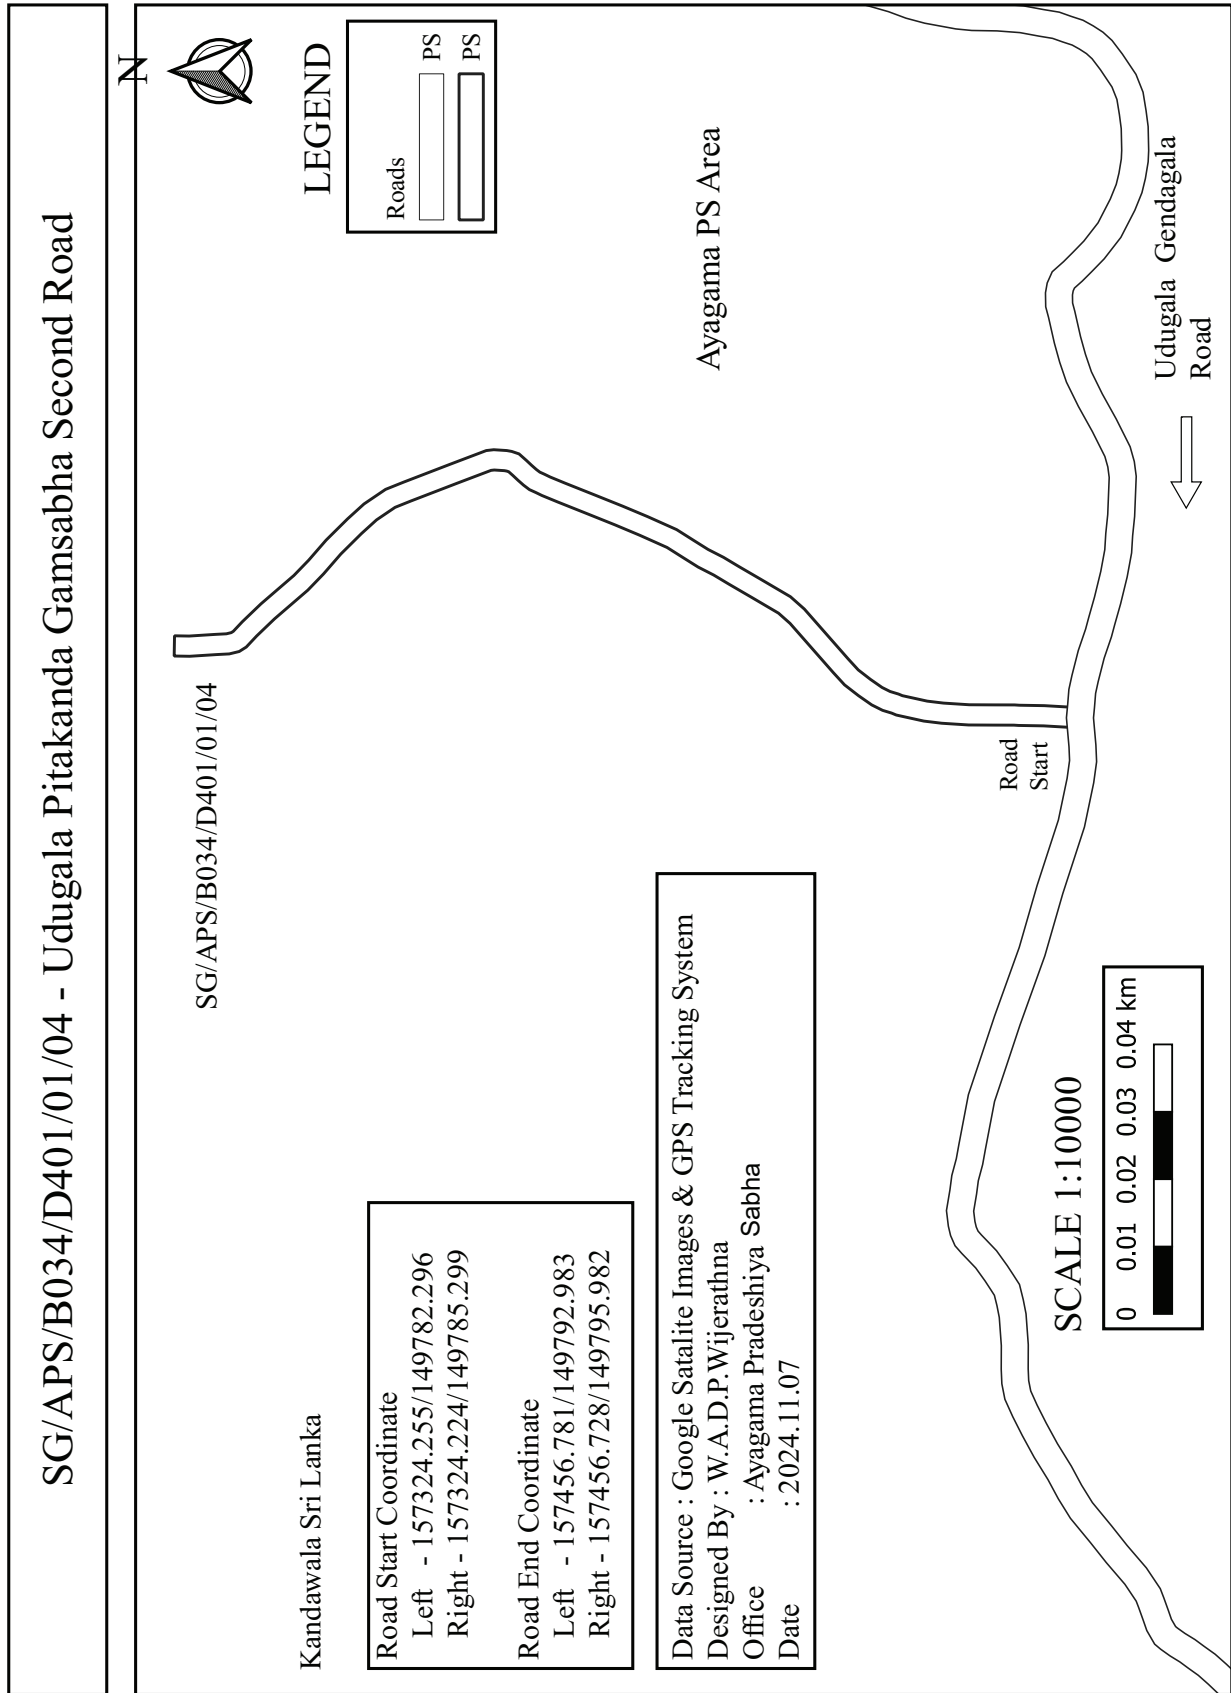


Data Source : Google Satalite Images & GPS Tracking System
Designed By : W.A.D.P.Wijerathna
Office : Ayagama Pradeshiya Sabha
Date : 2024.11.07

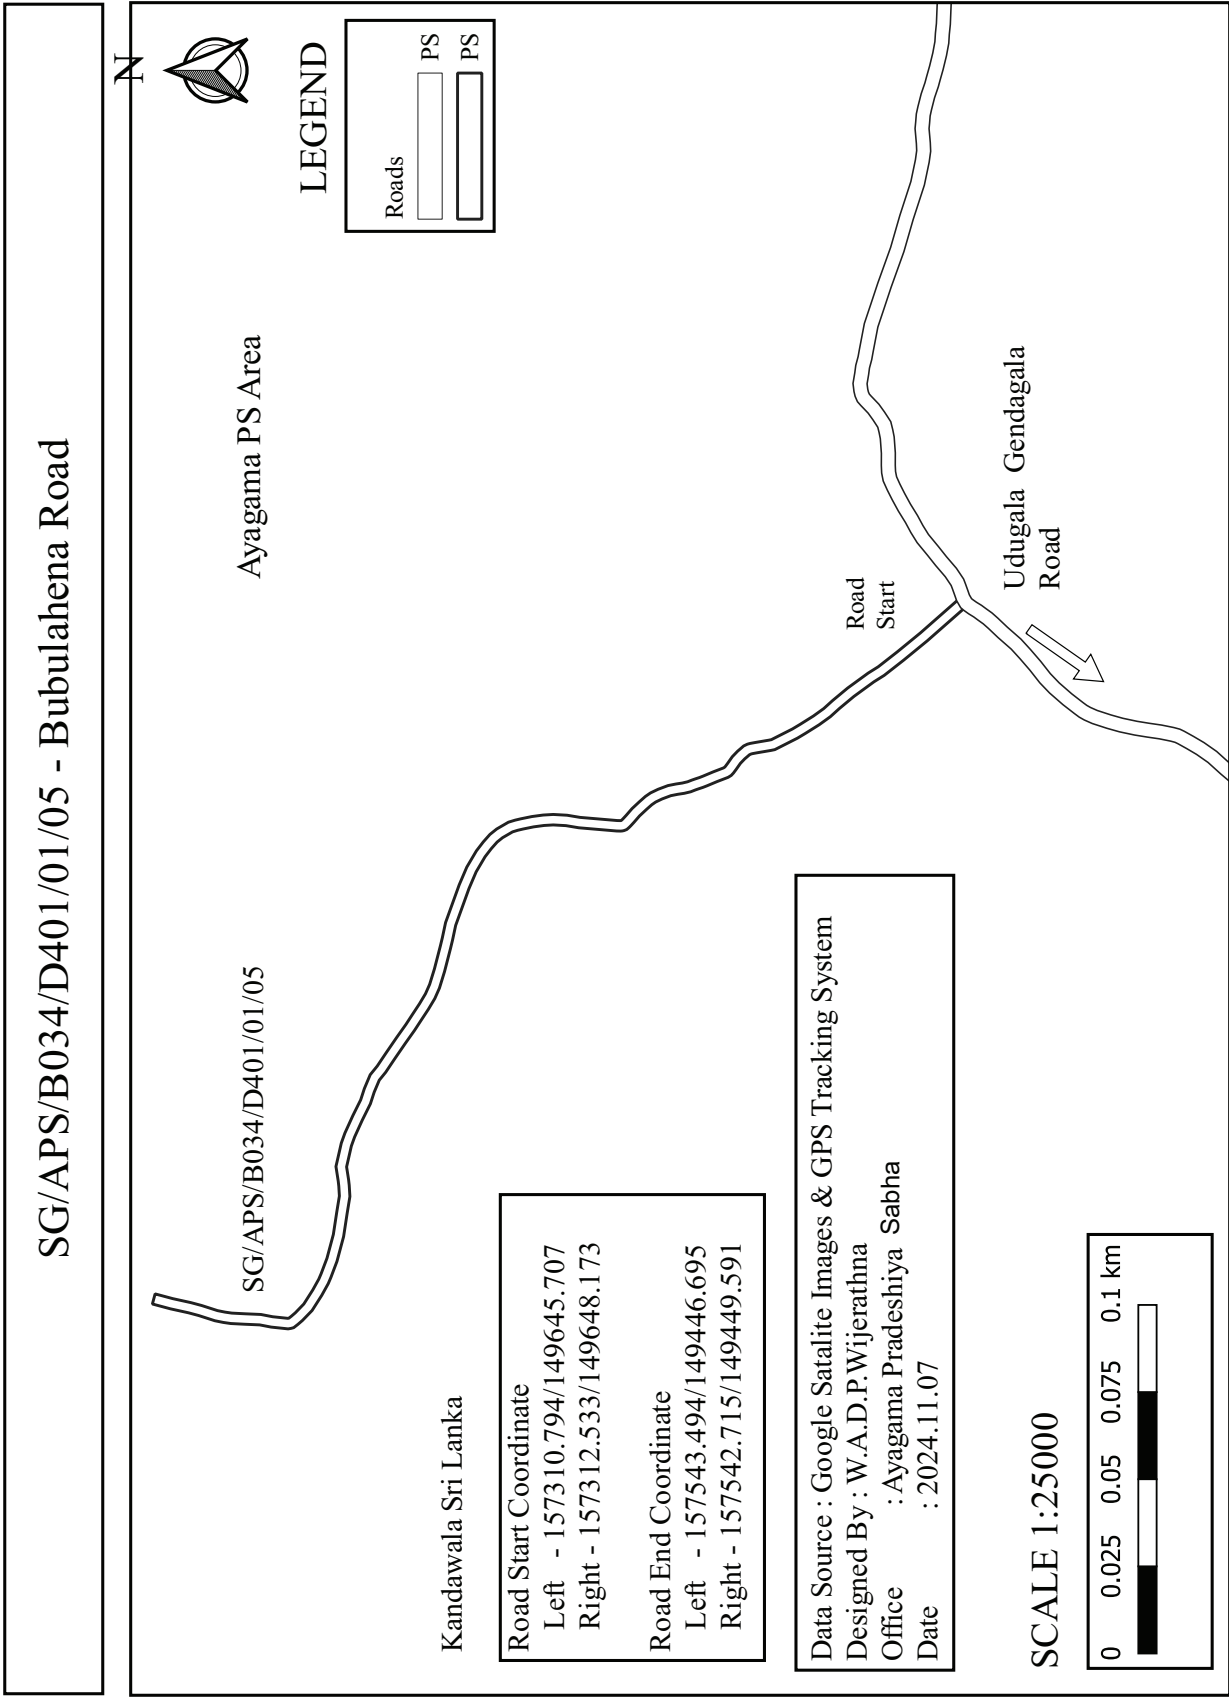

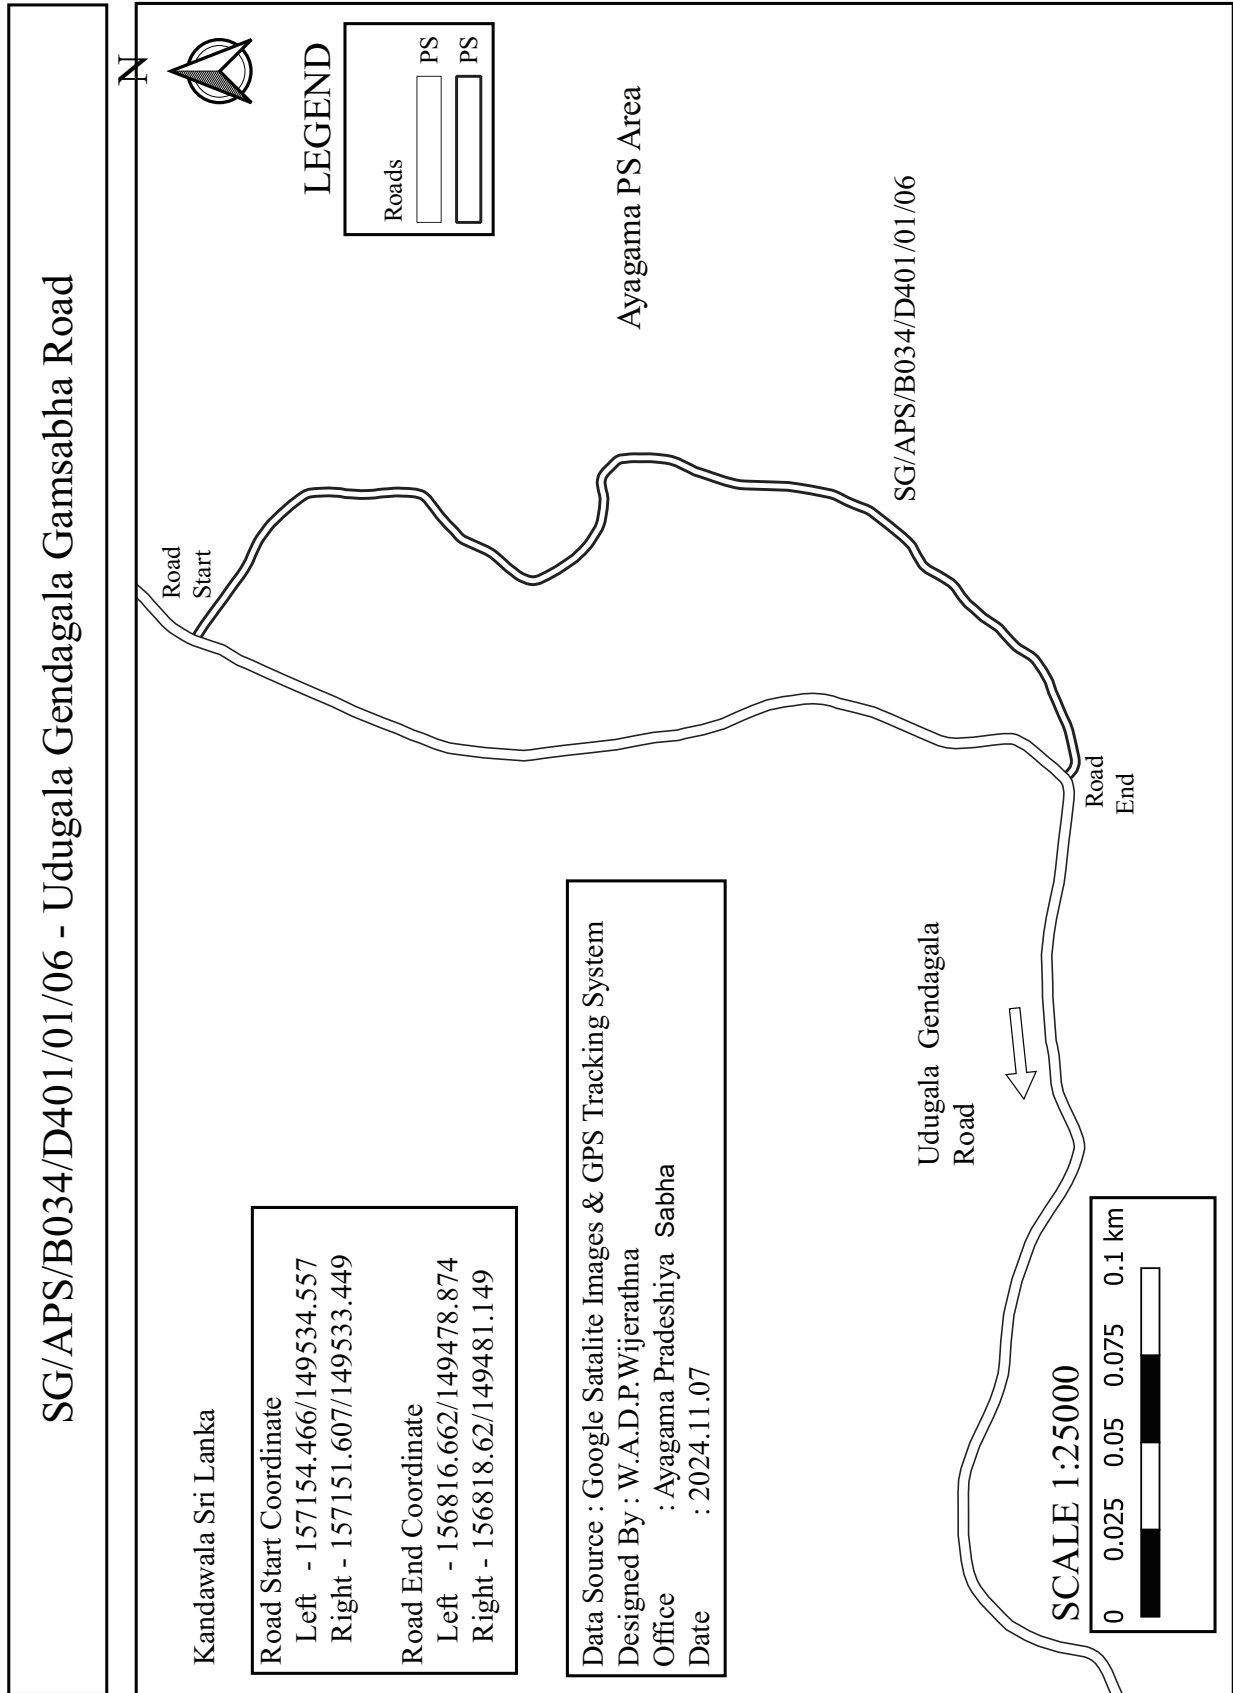

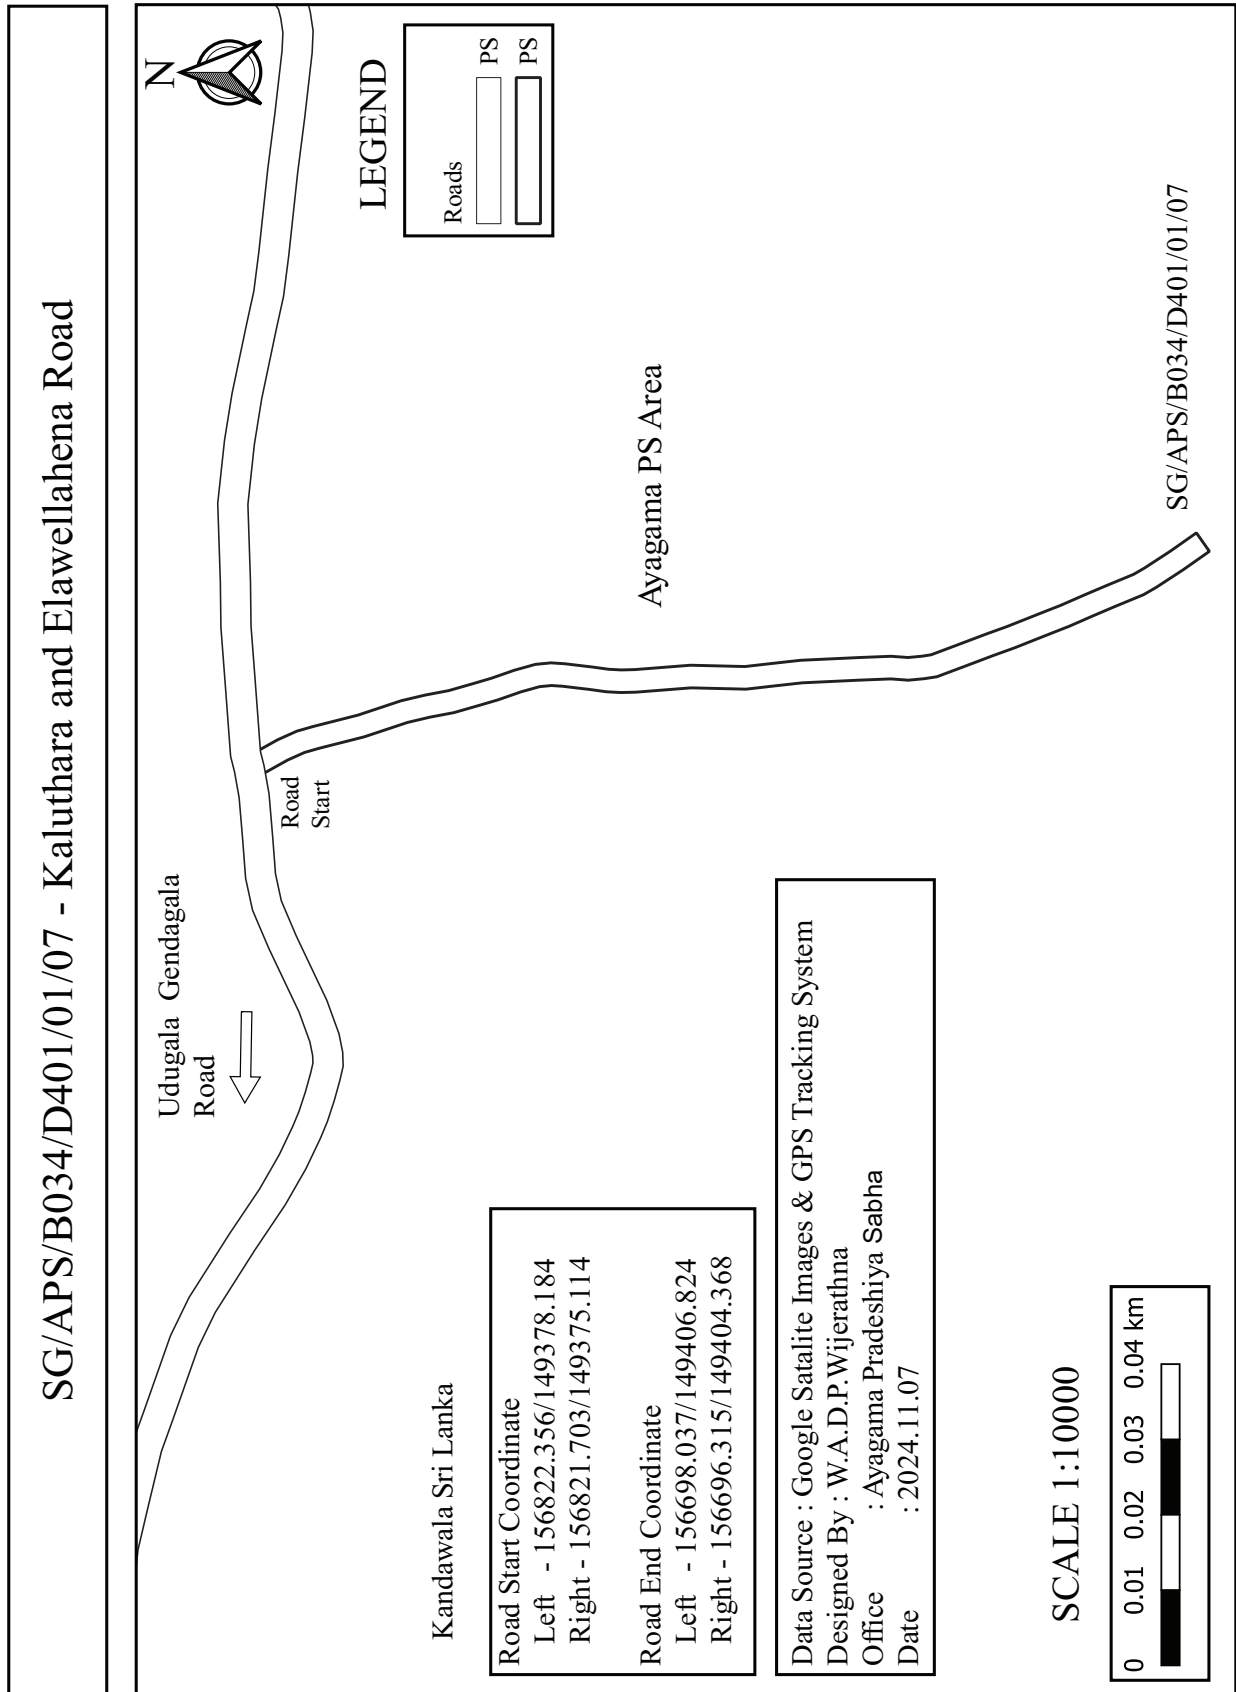



SG/APS/B034/D401/01/08 - First Lane of Udugala Gendagala Road

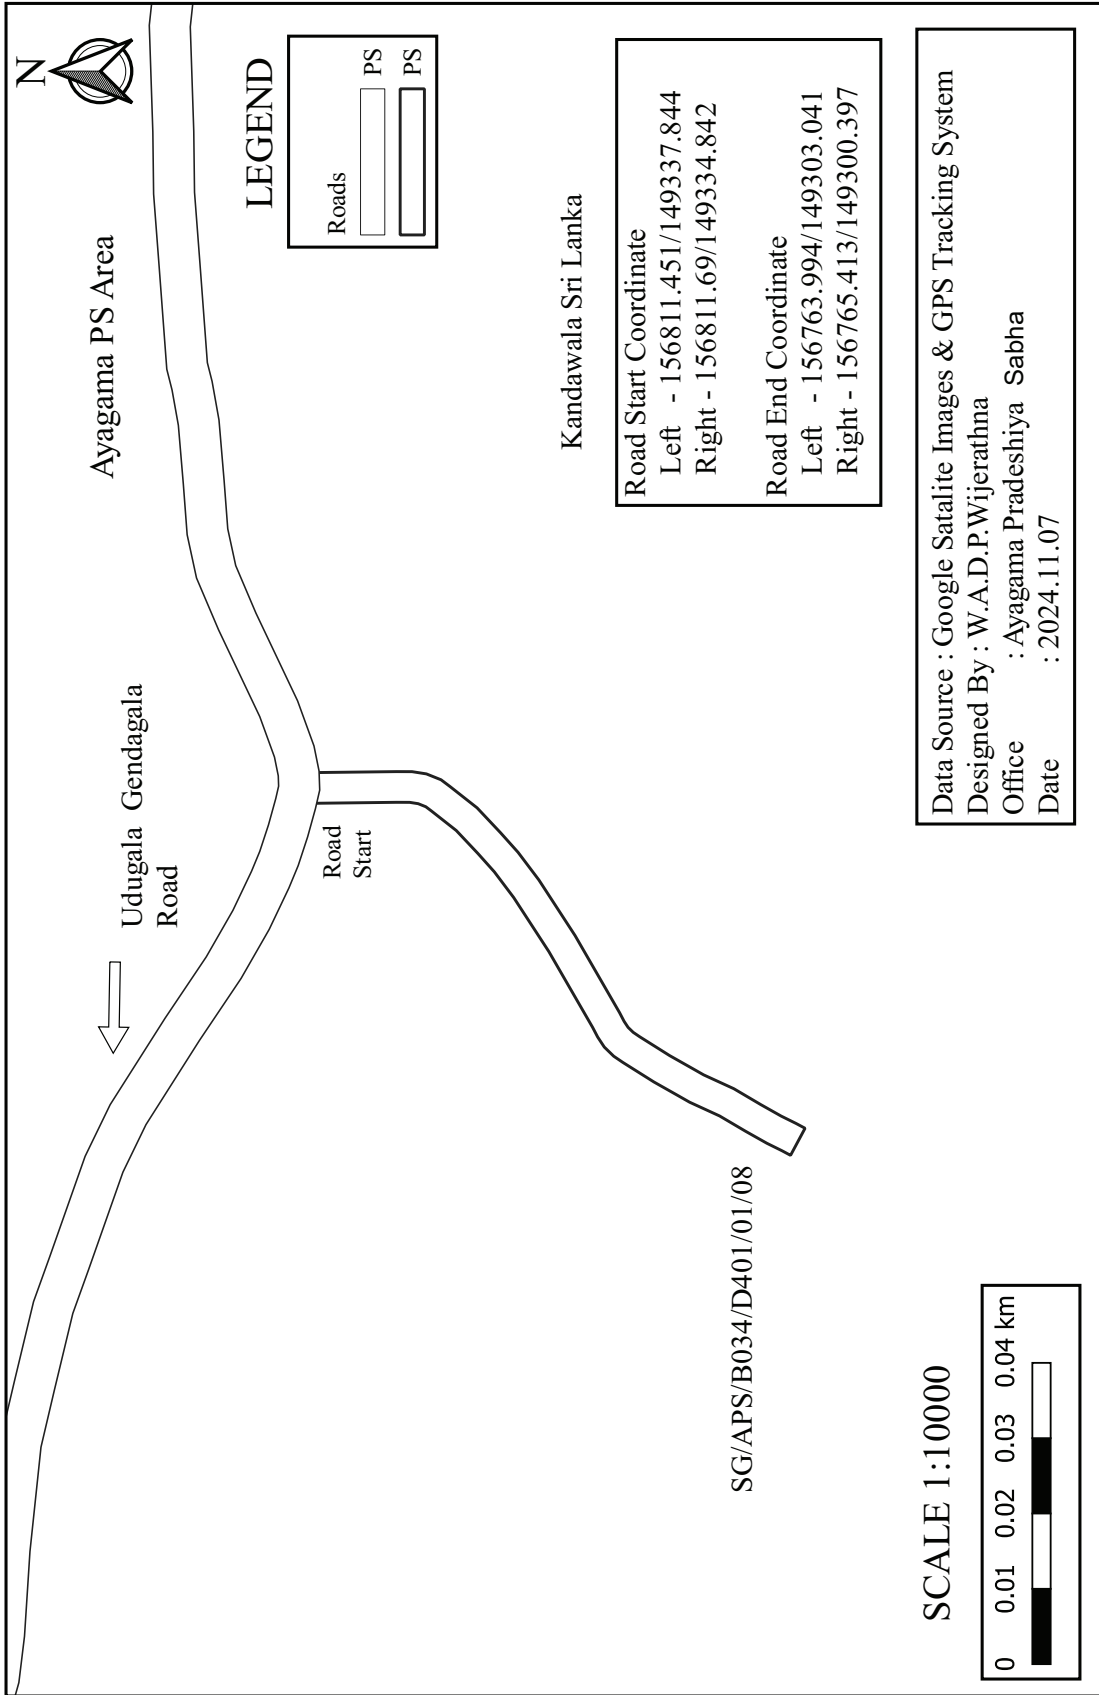





SG/APS/B034/D401/01/10 - Gendagala Aranya Road

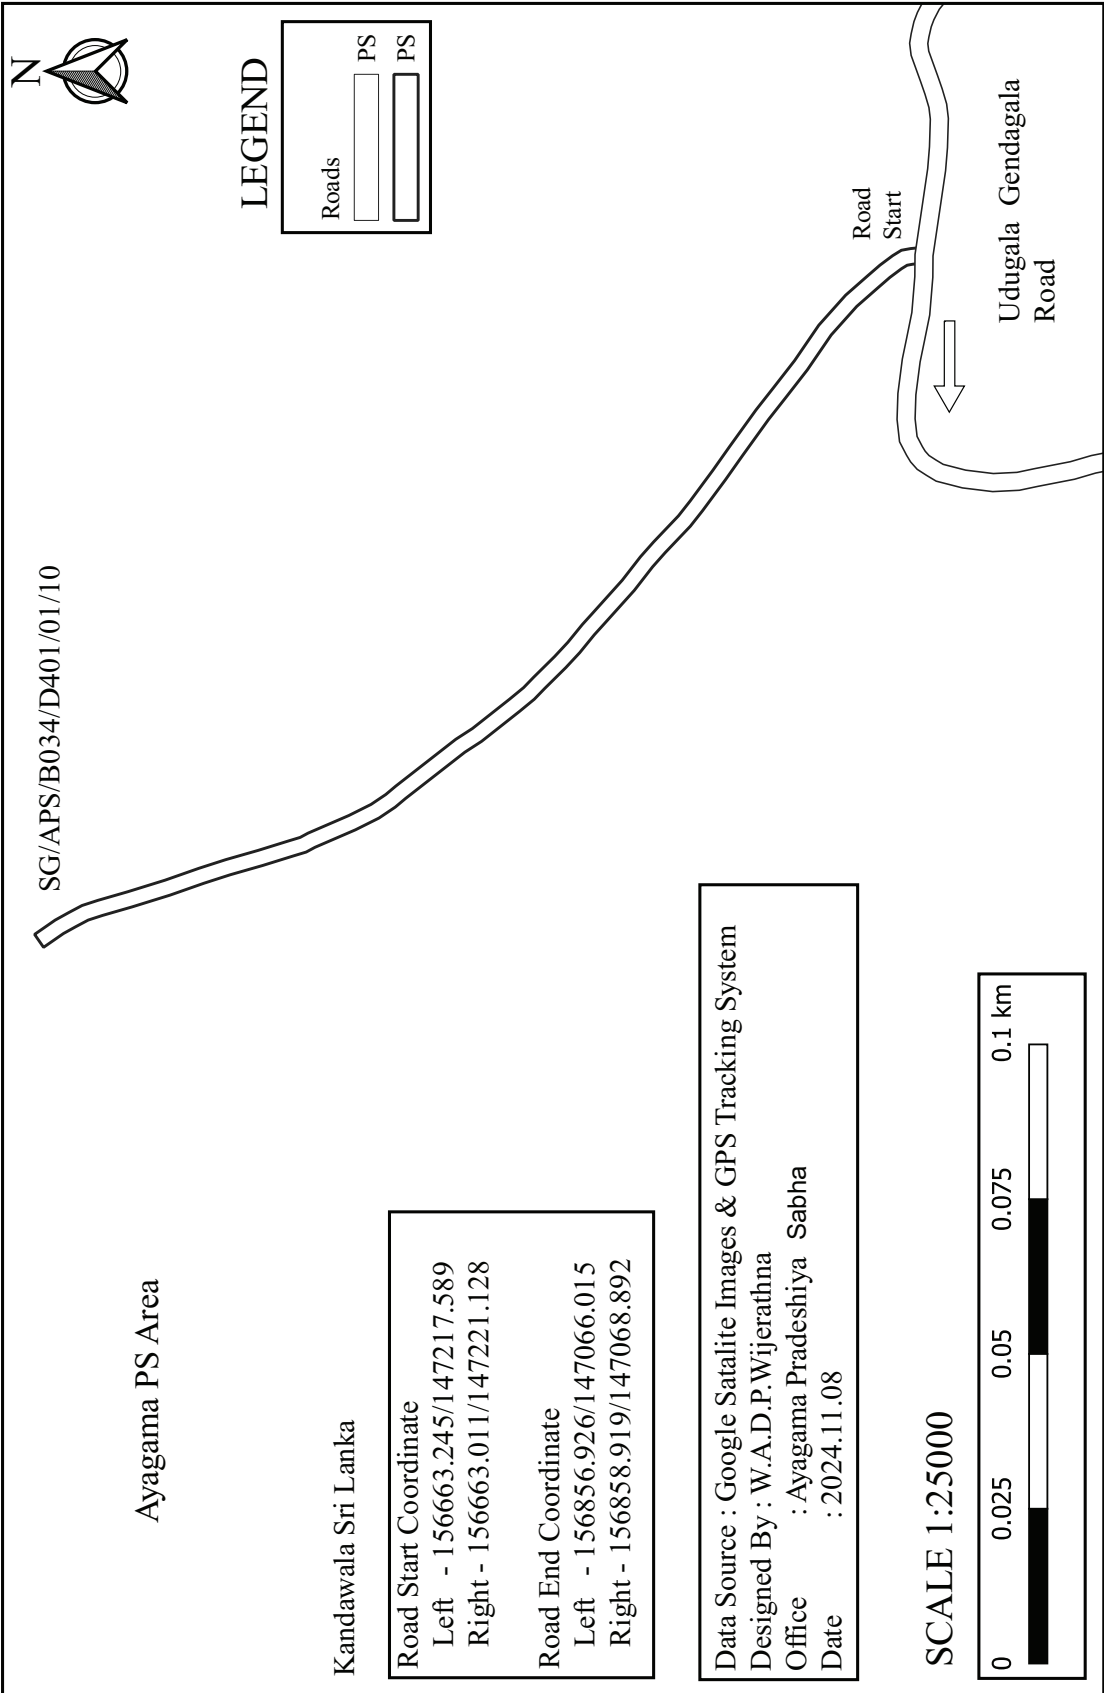

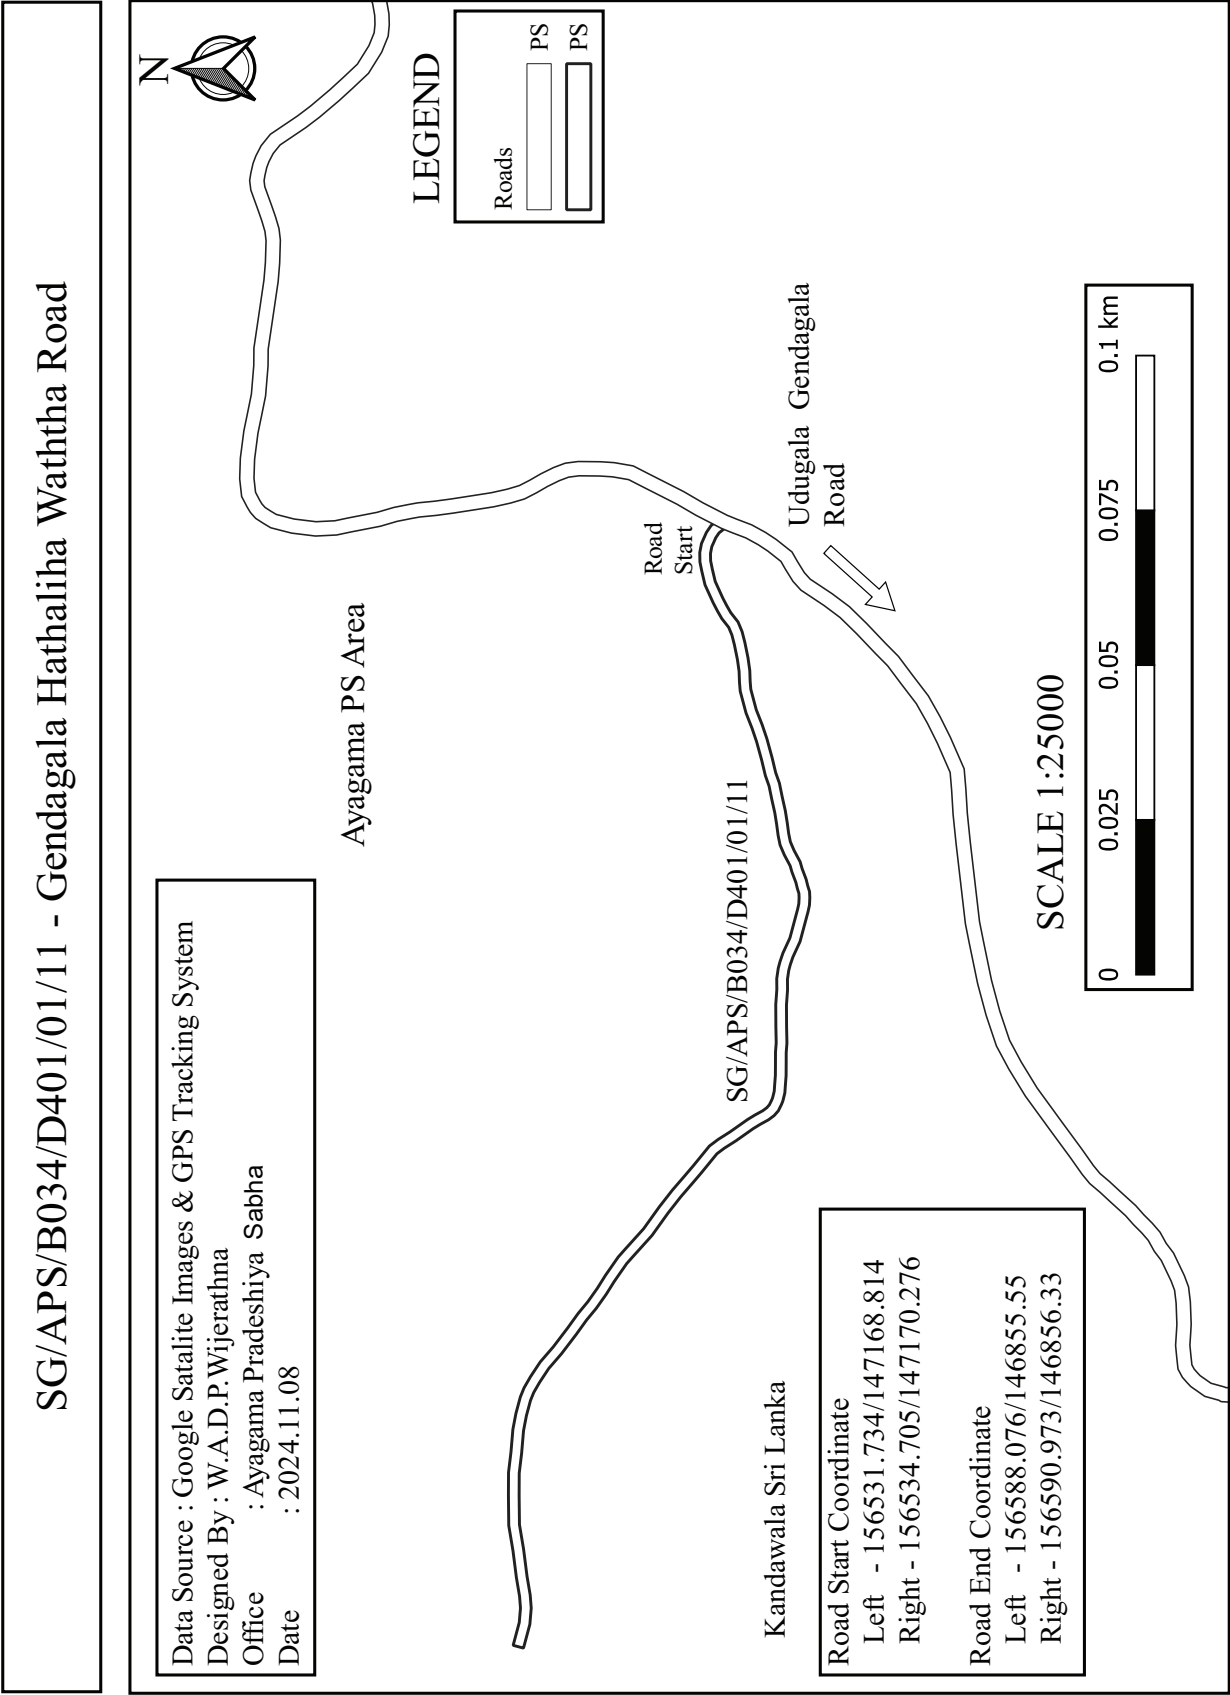



SG/APS/B034/D401/01/12 - Gendagala Millahena Footpath

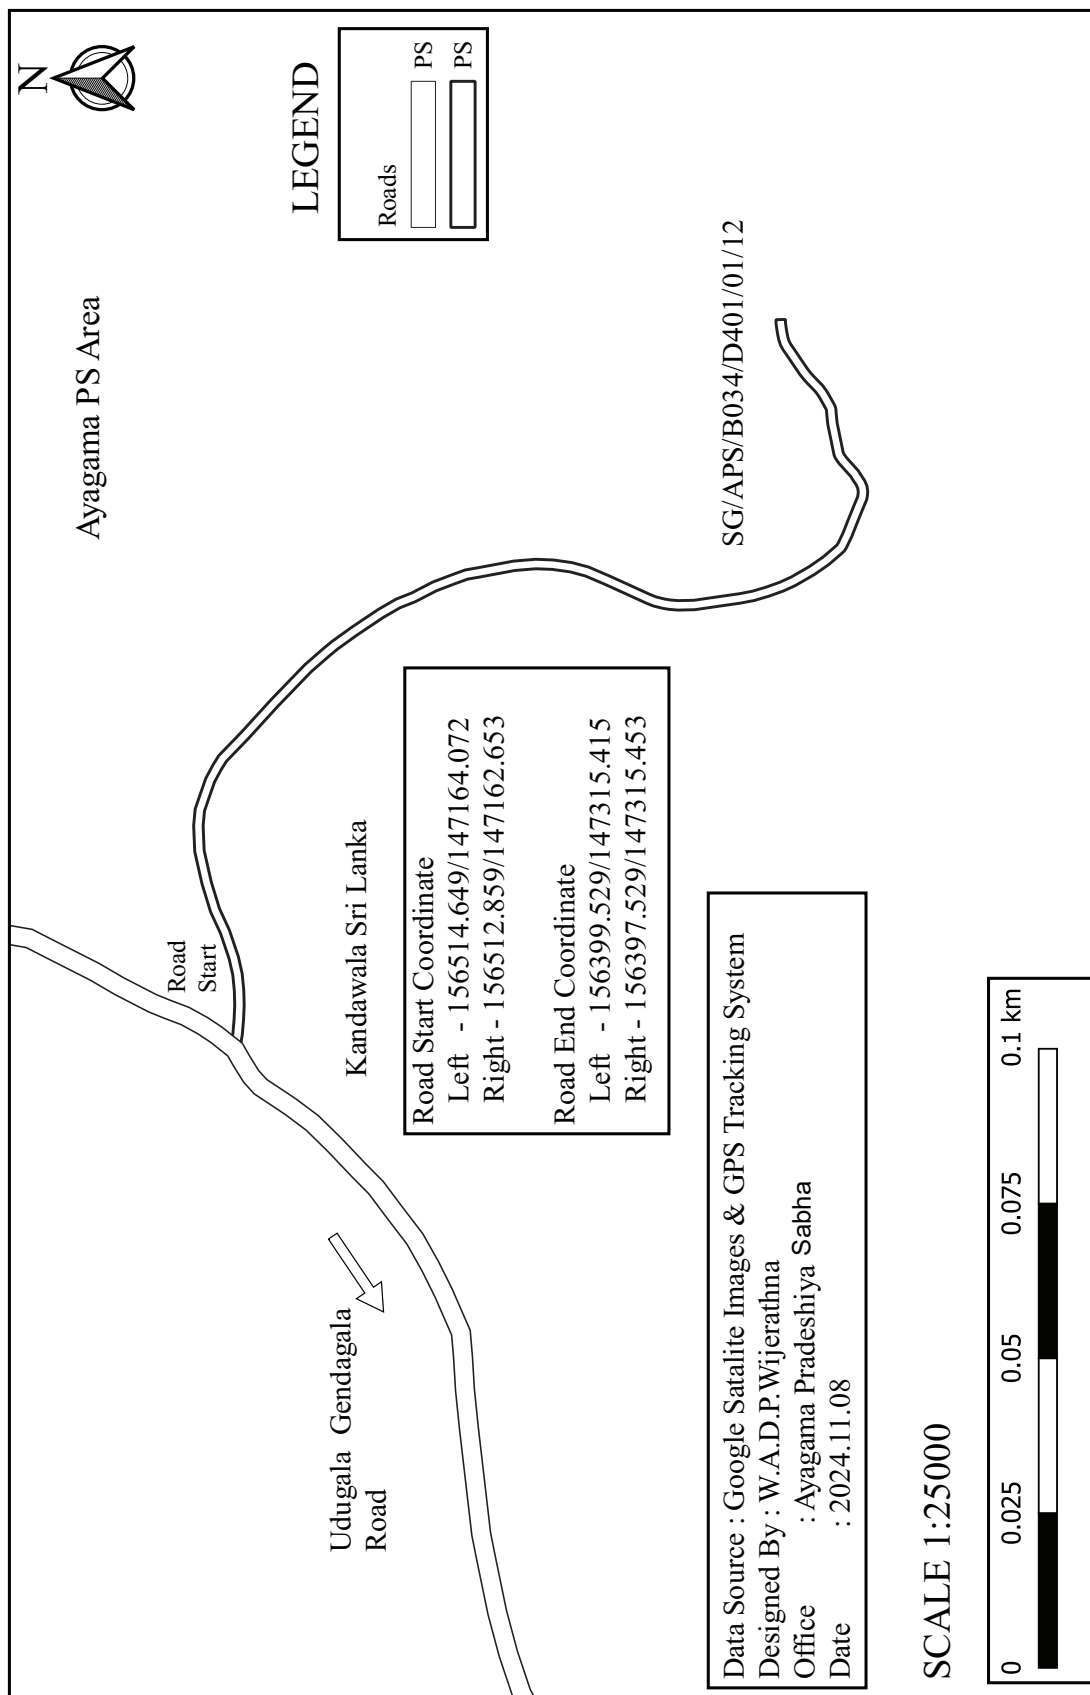


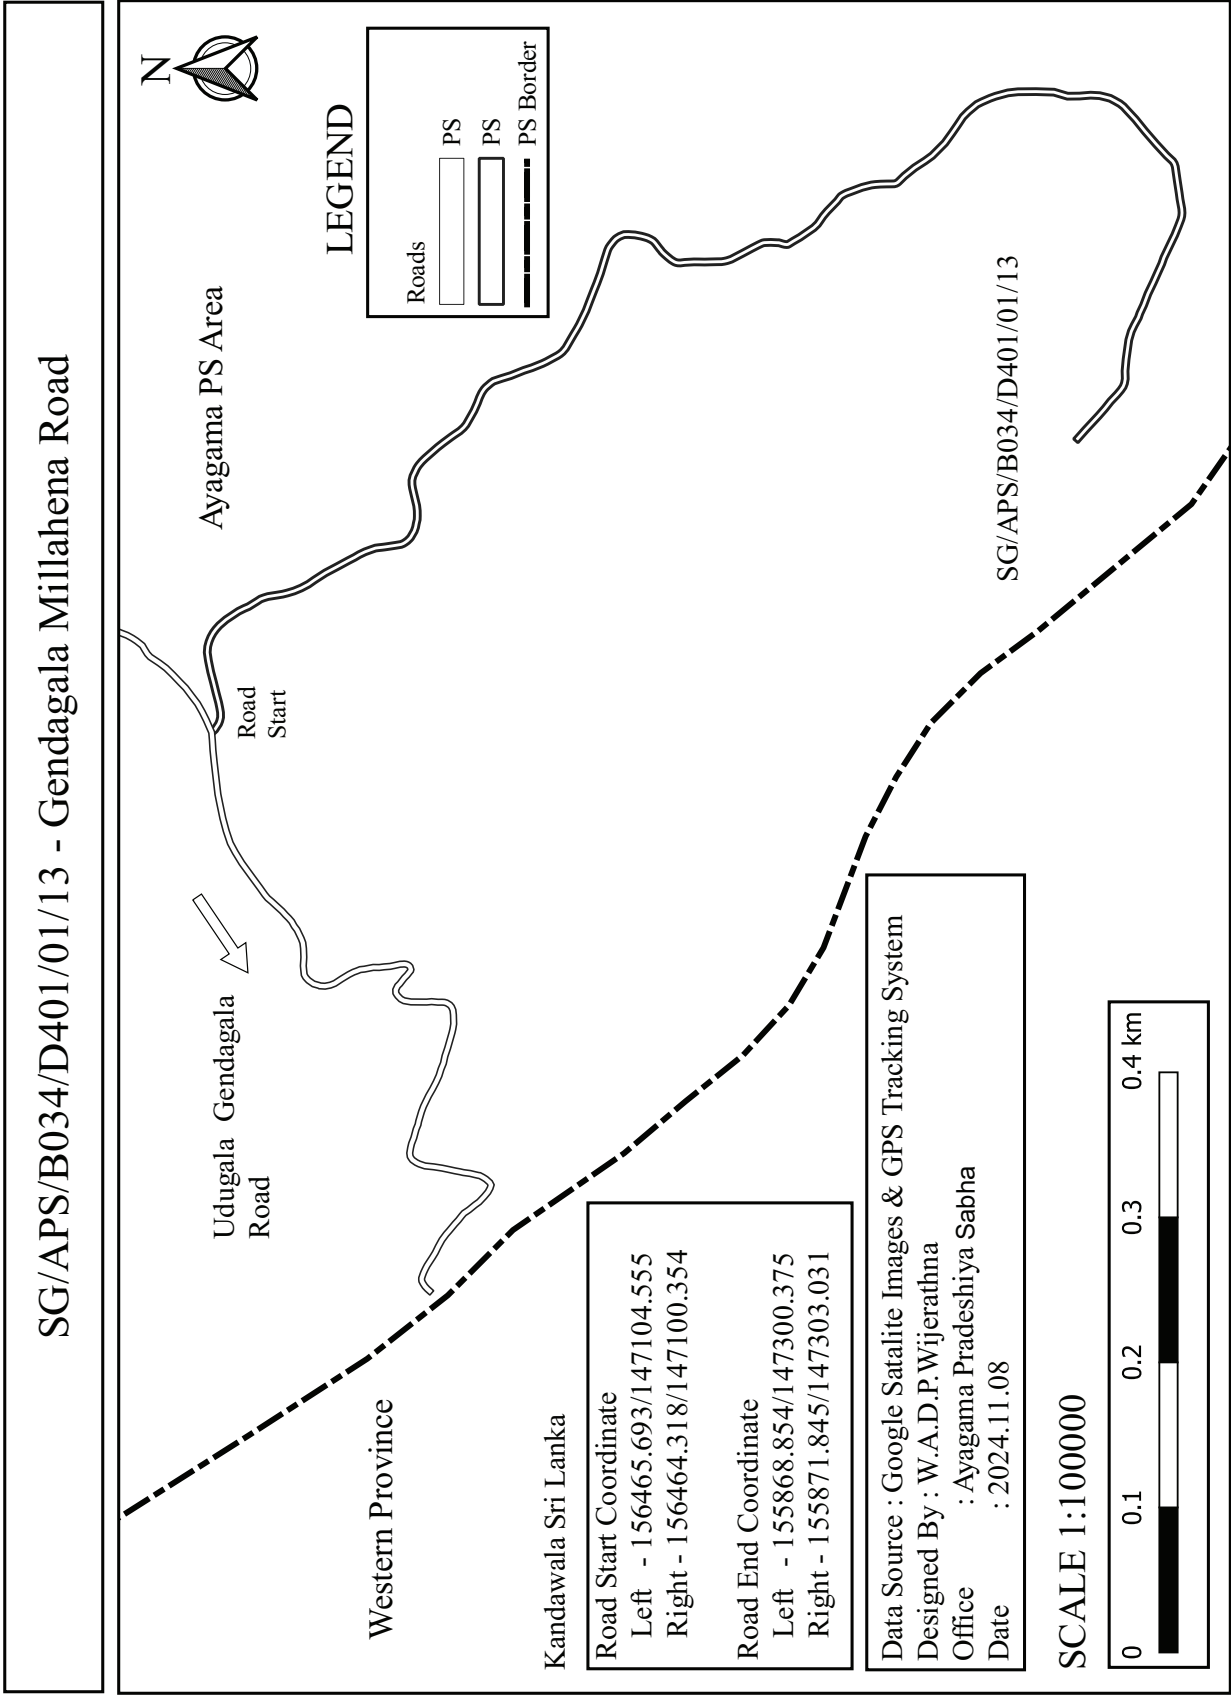


SG/APS/B034/D401/01/13/01 - First Lane of Gendagala Millahena Road

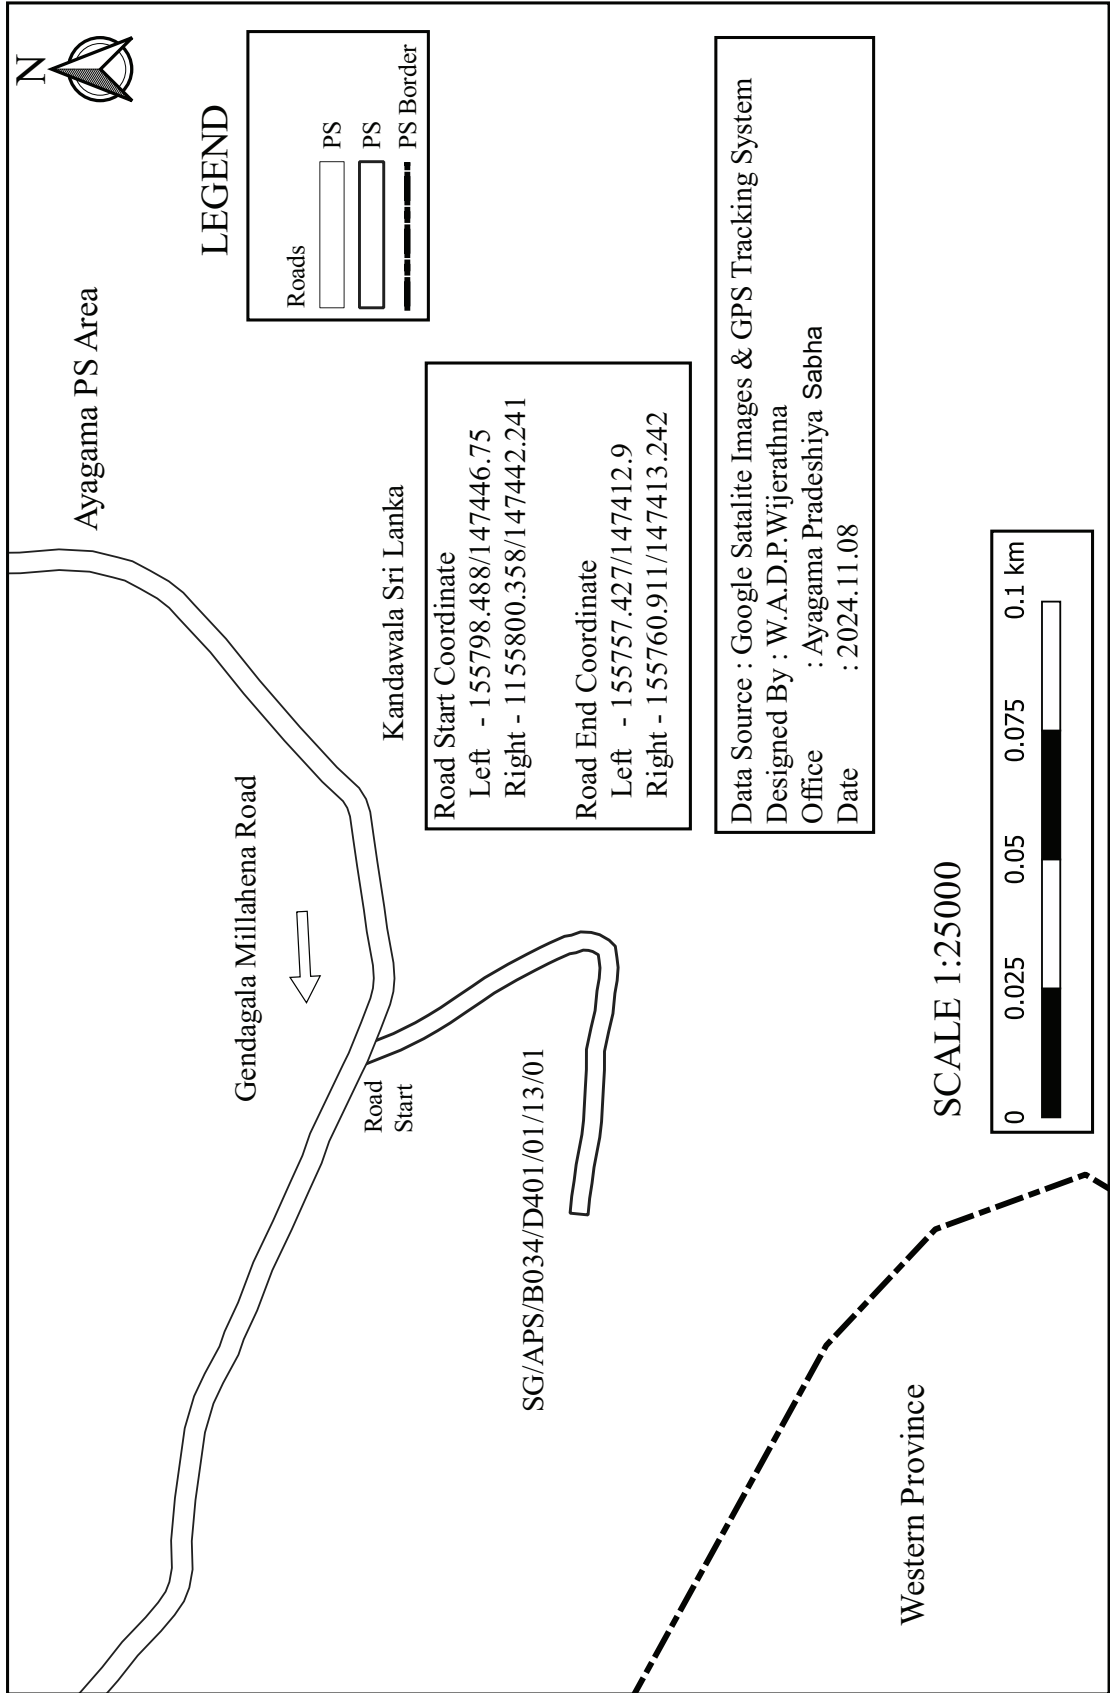

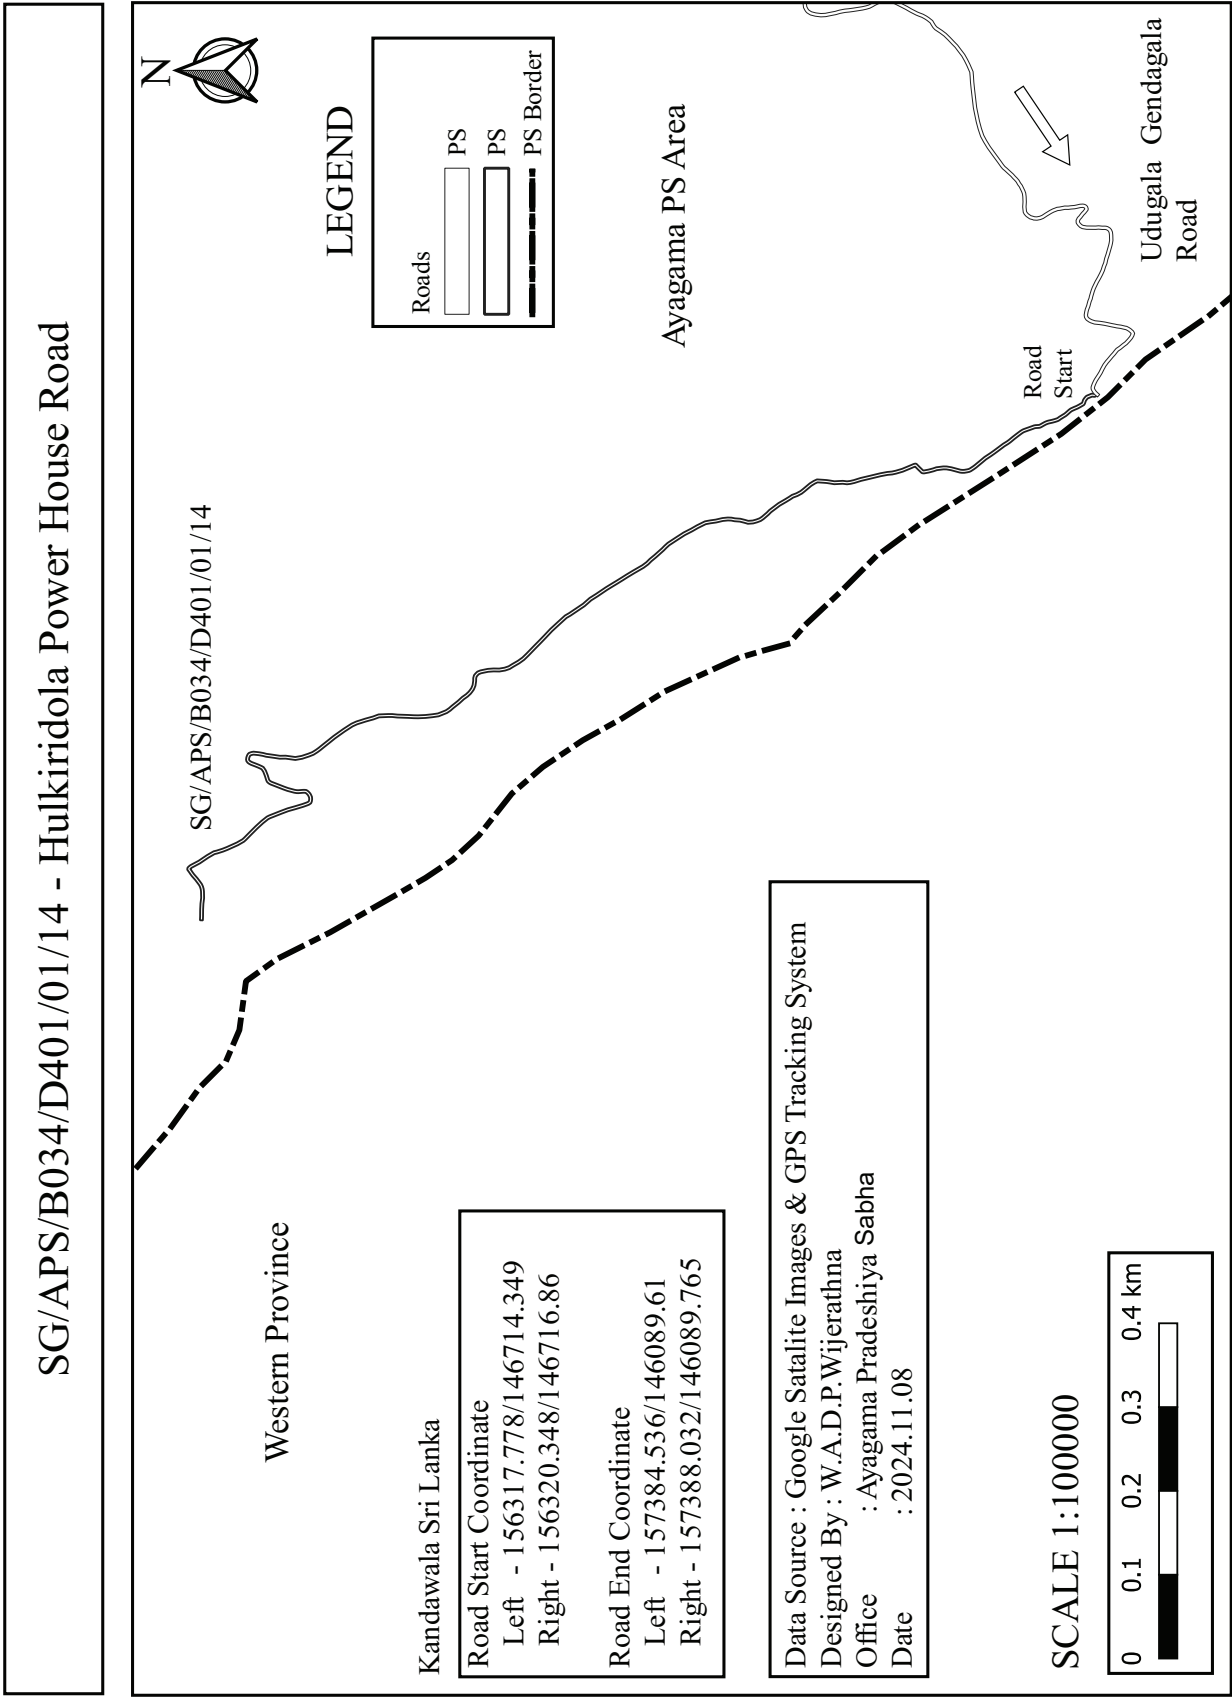


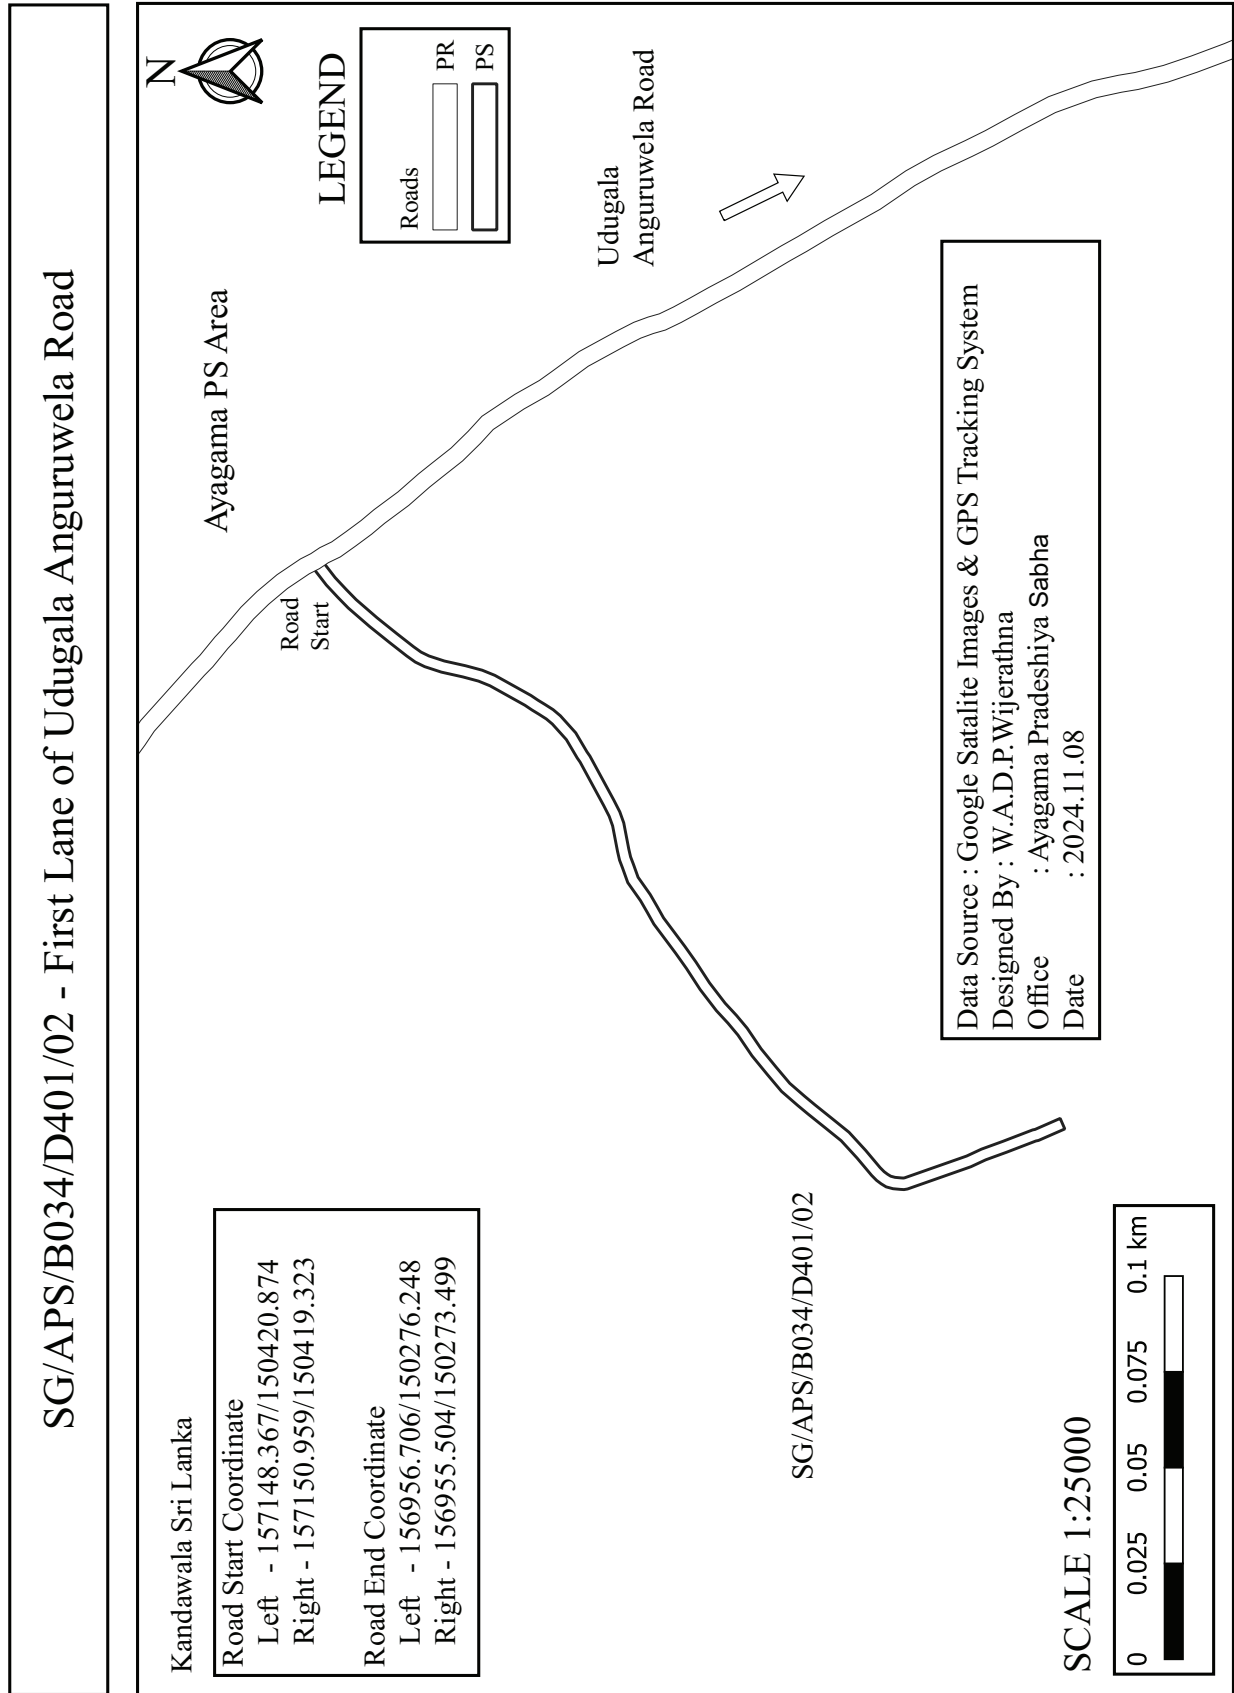



Data Source : Google Satalite Images & GPS Tracking System
 Designed By : W.A.D.P.Wijerathna
 Office : Ayagama Pradeshiya Sabha
 Date : 2024.11.08

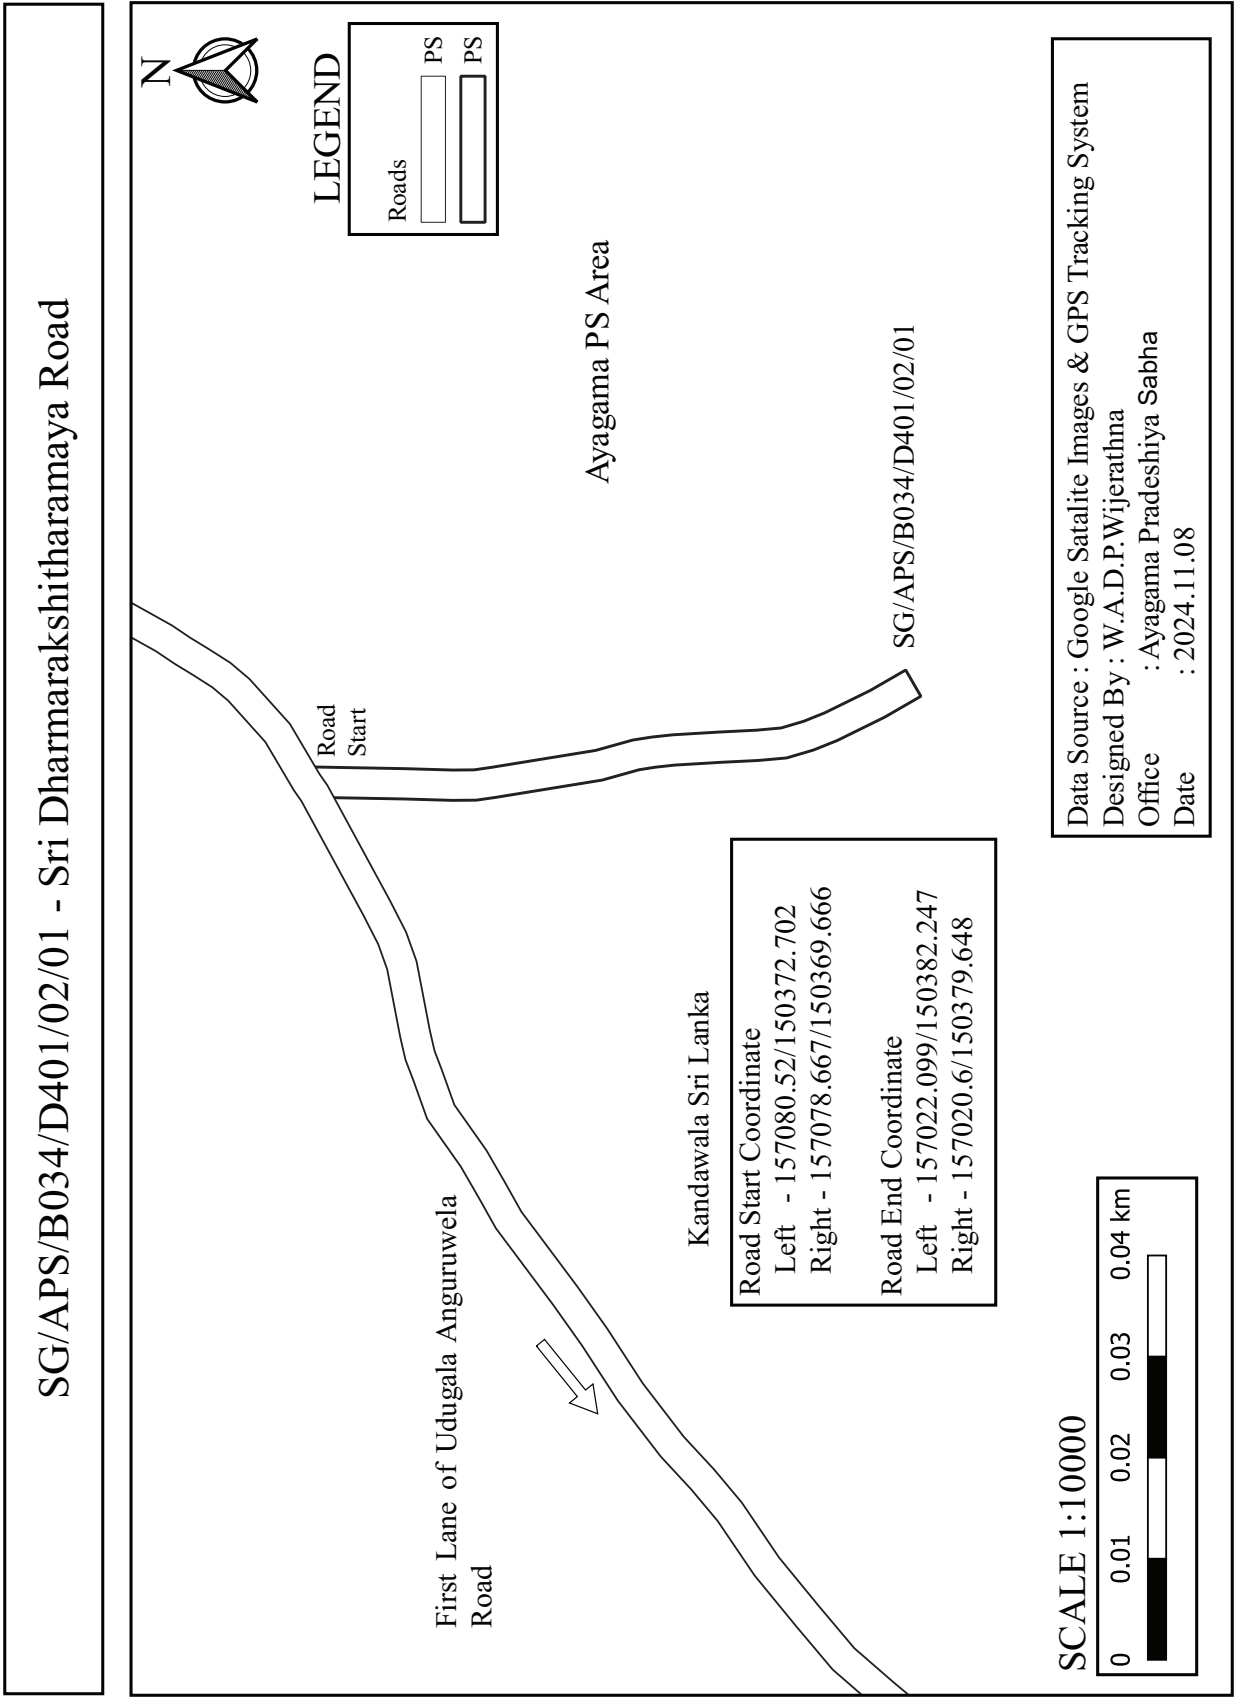


SG/APS/B034/D401/03 - Second Lane of Udugala Anguruwela Road

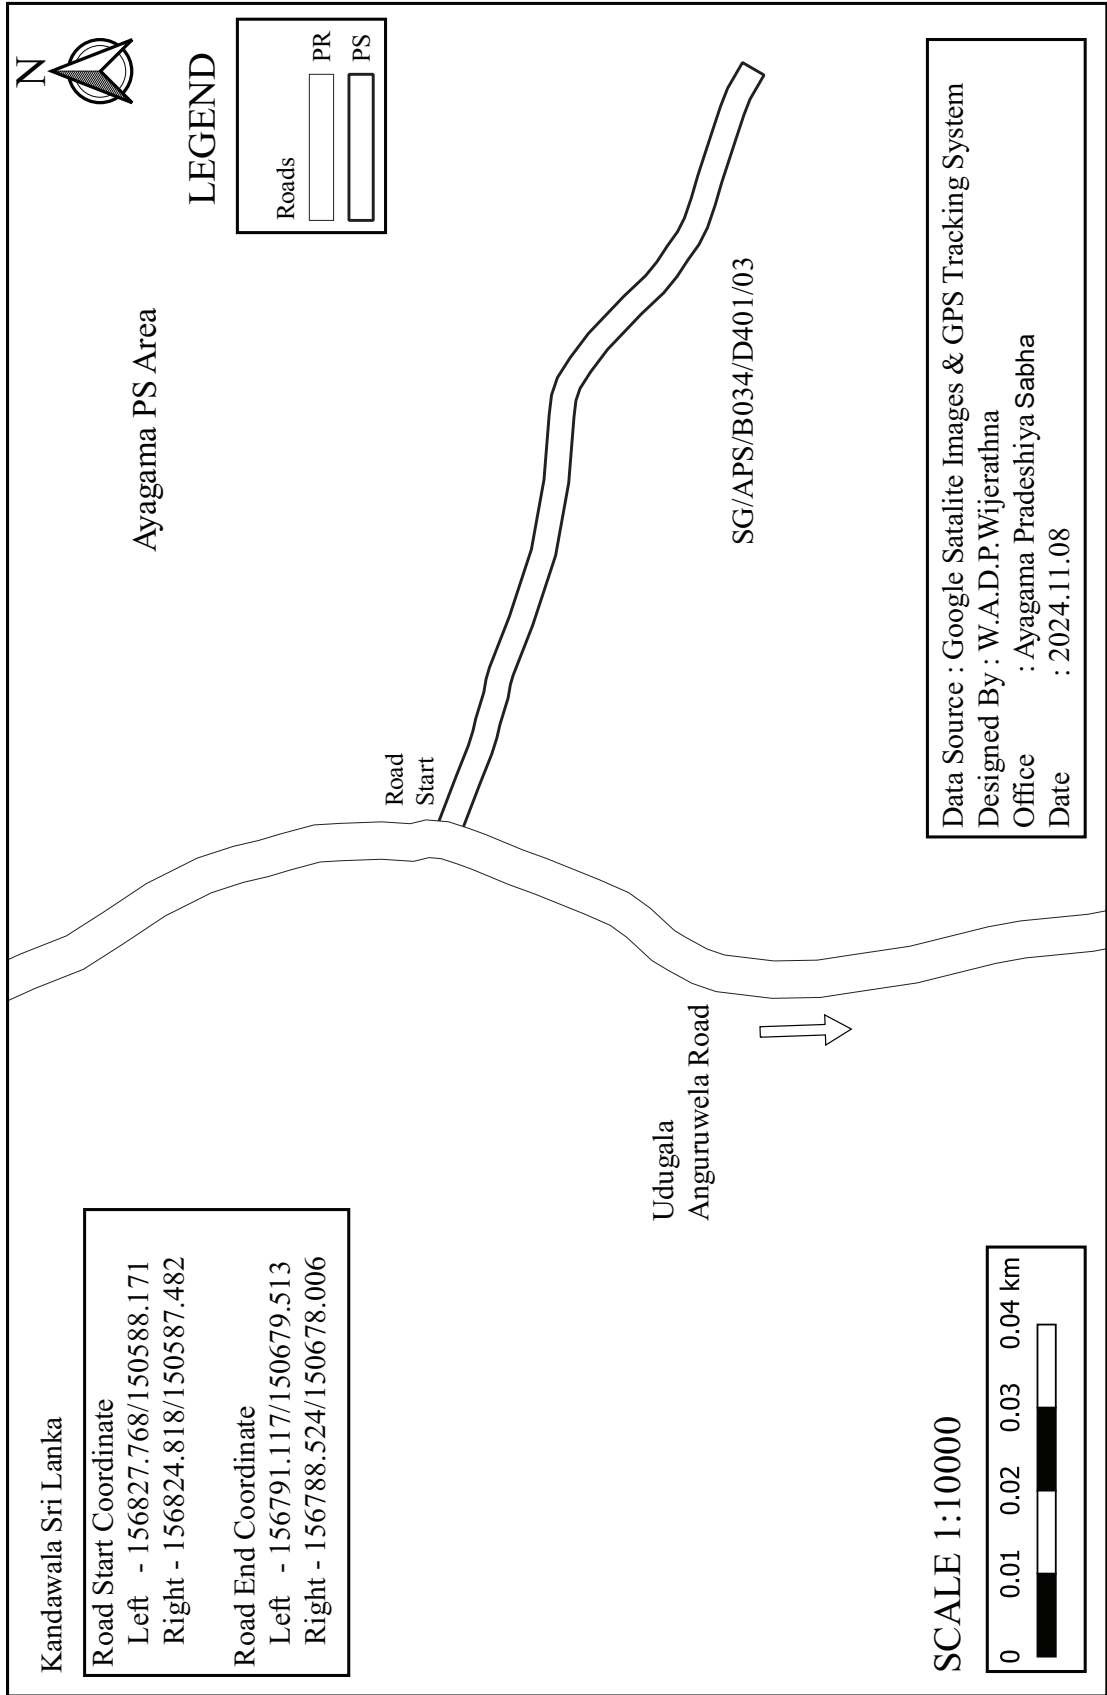


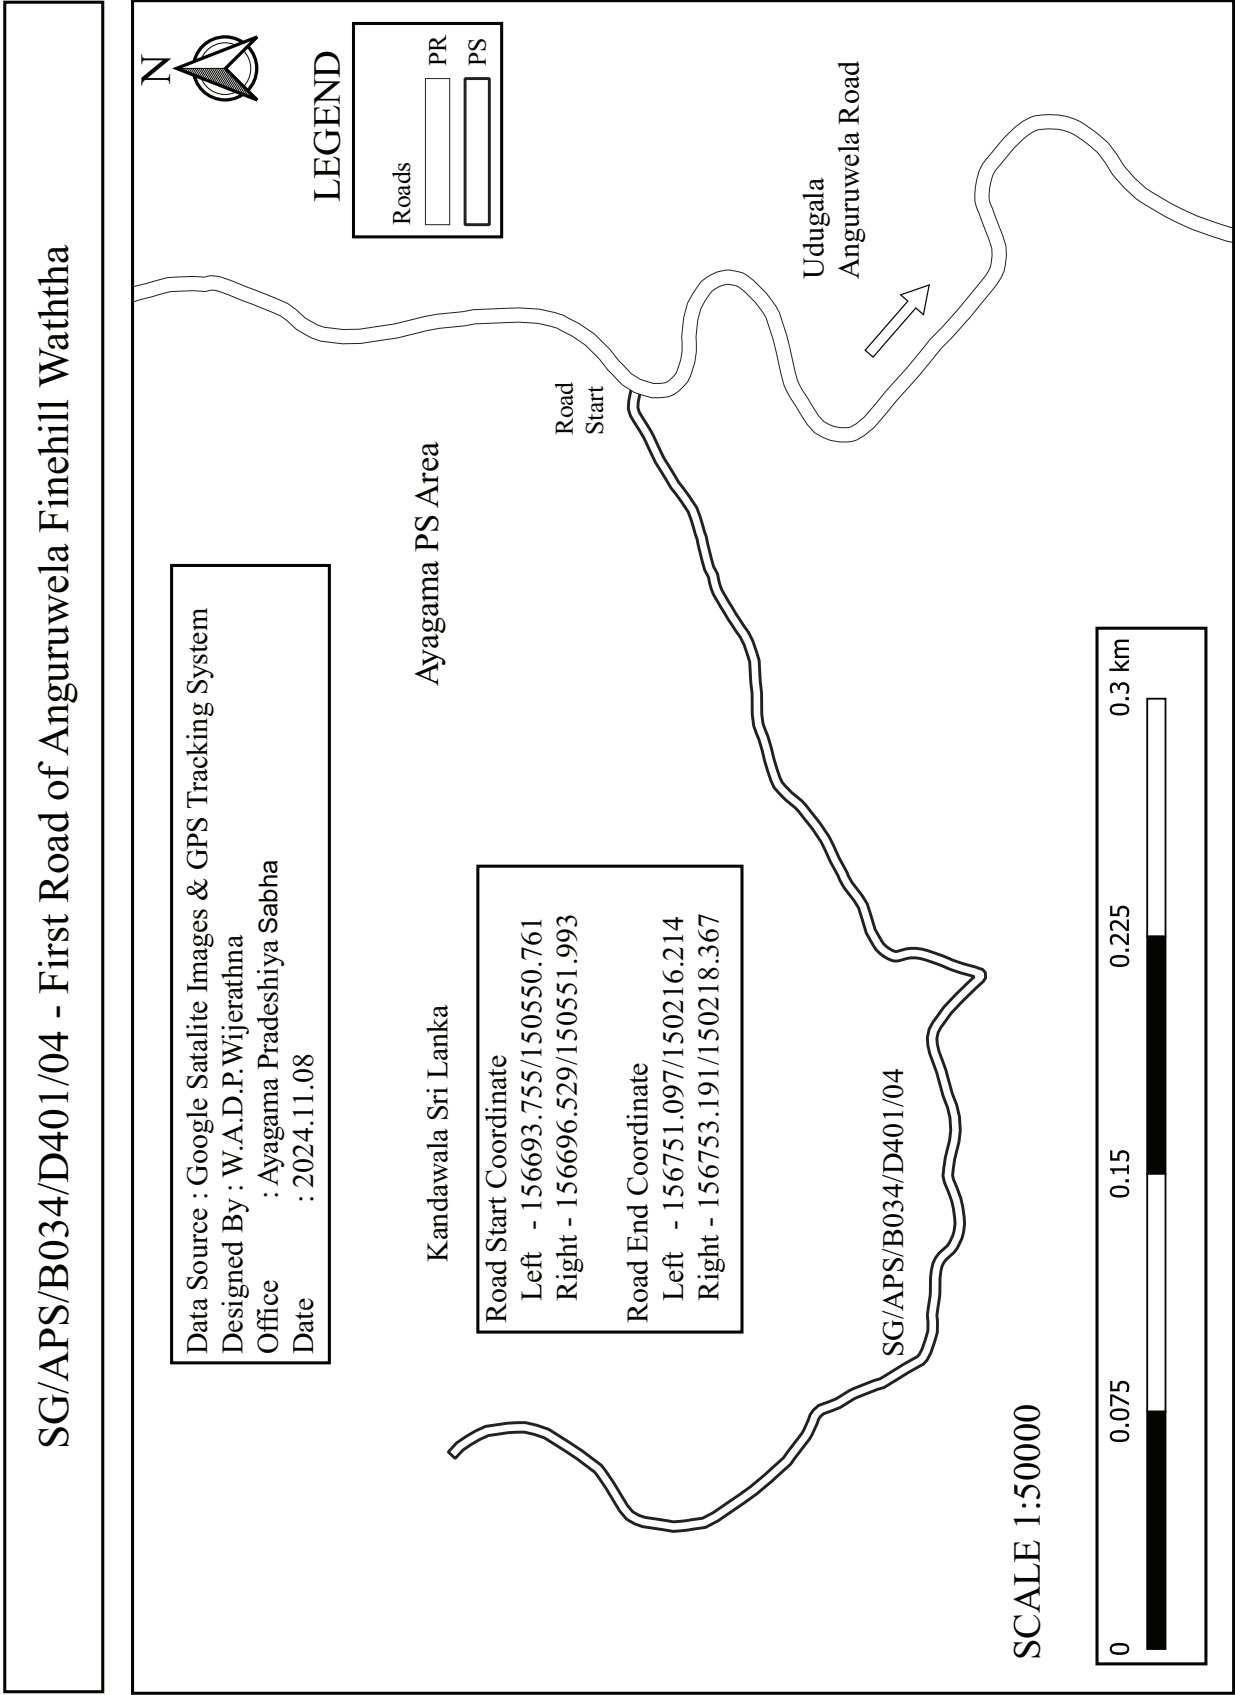


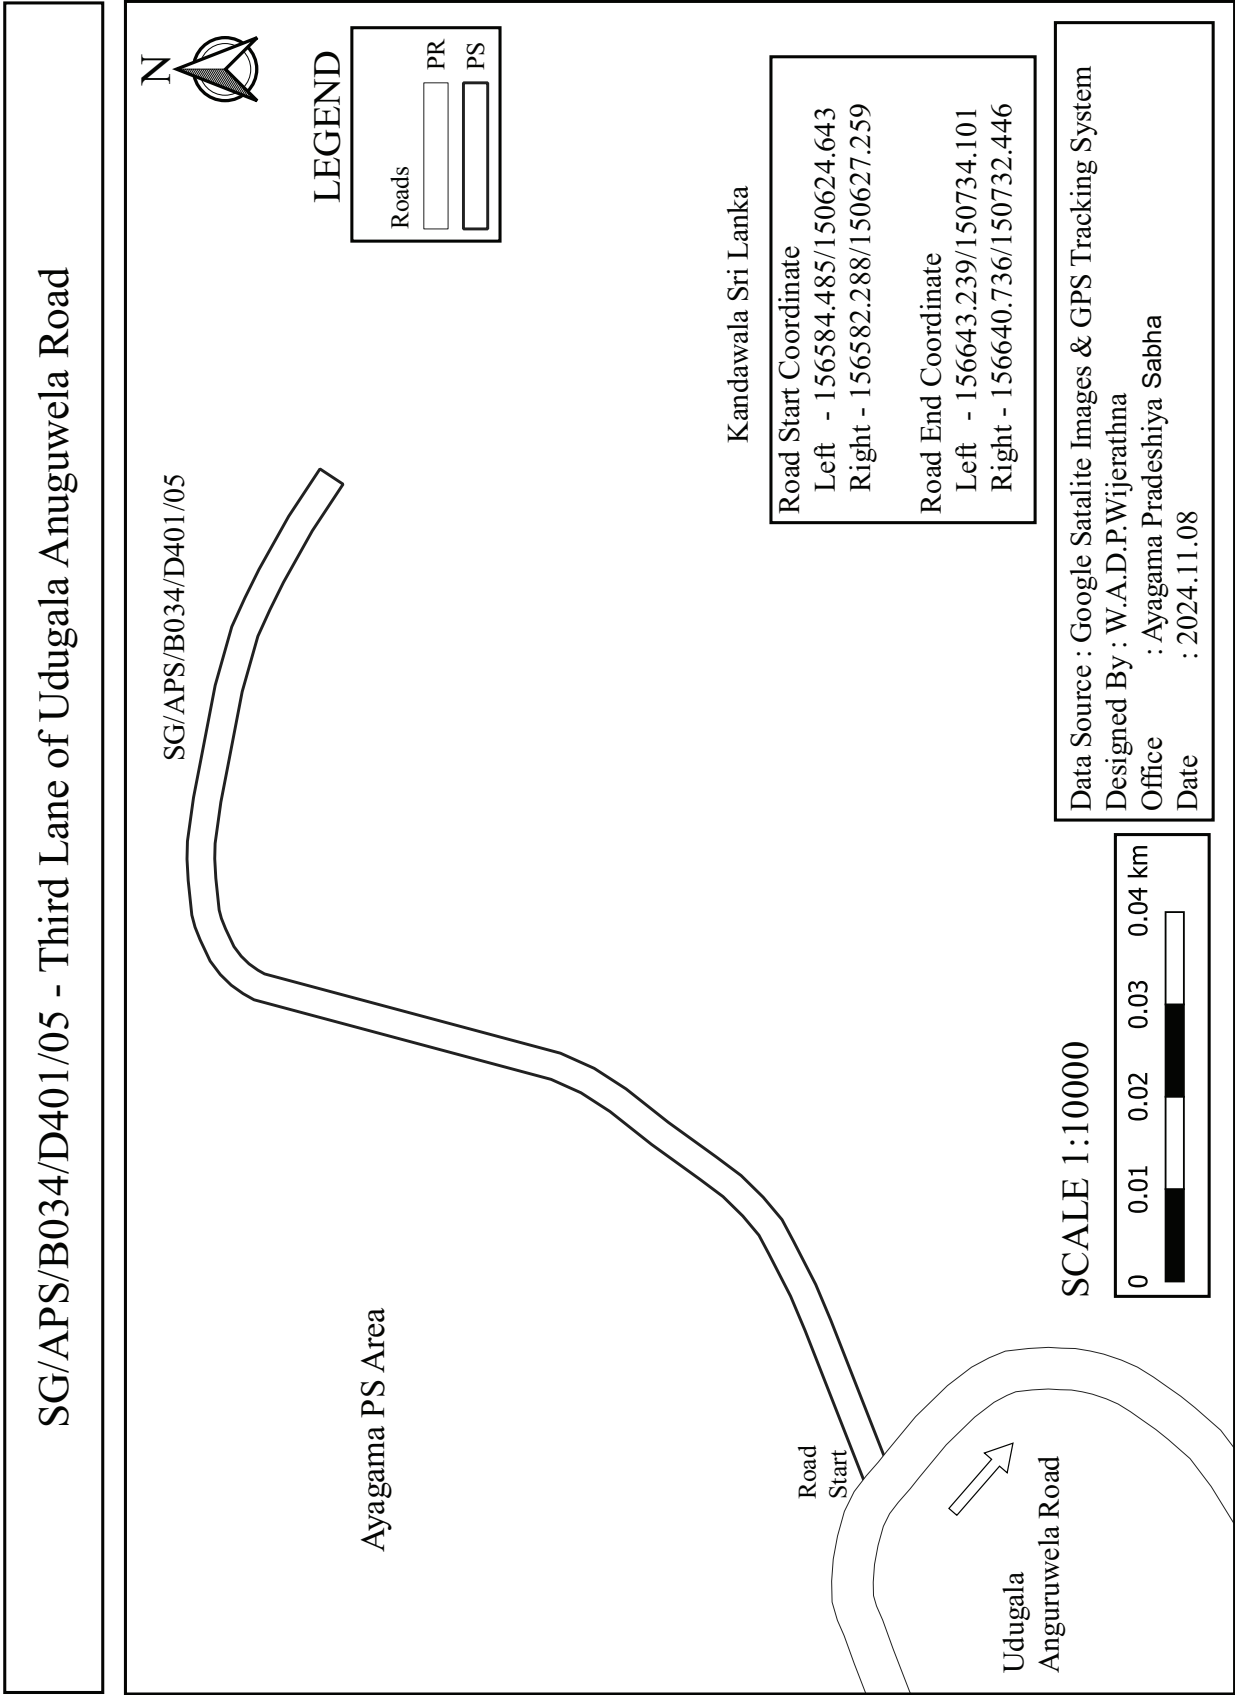

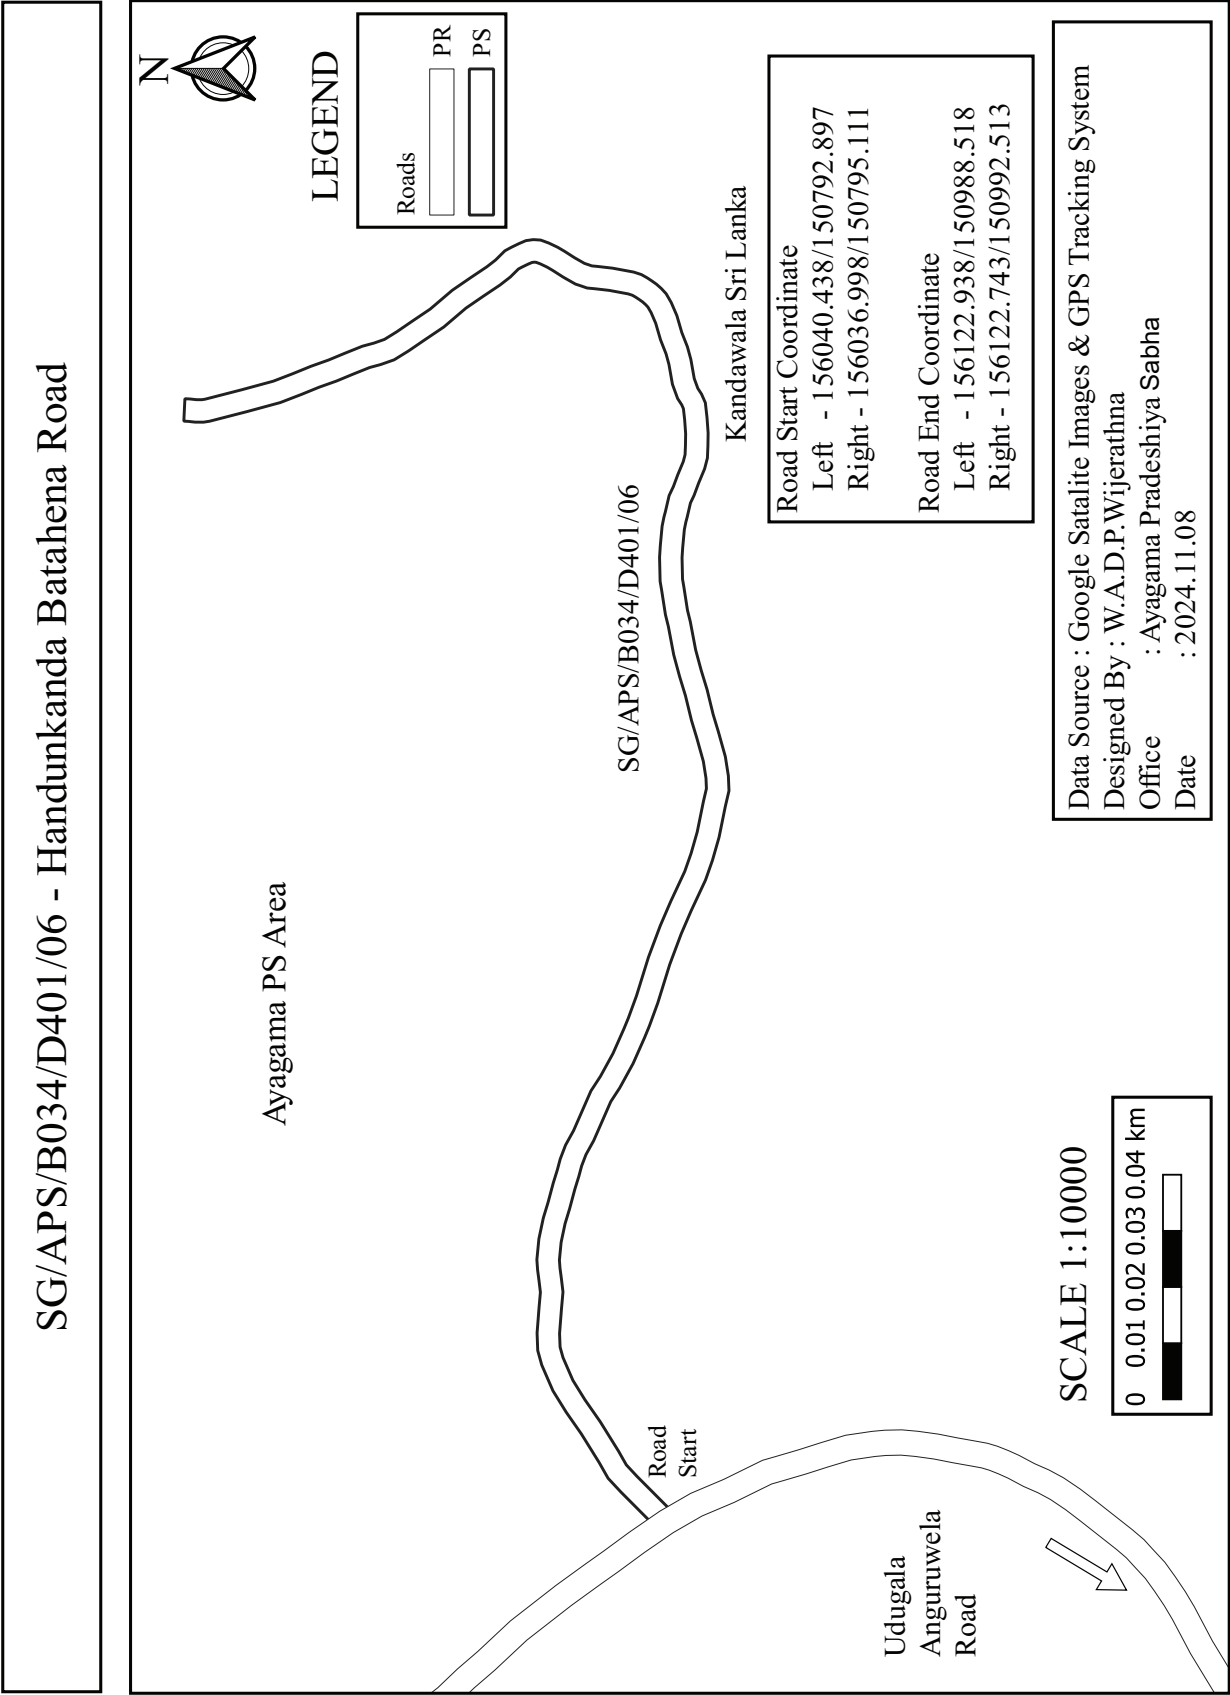



SG/APS/B034/D401/06/01 - First Lane of Handunkanda Batahena Road

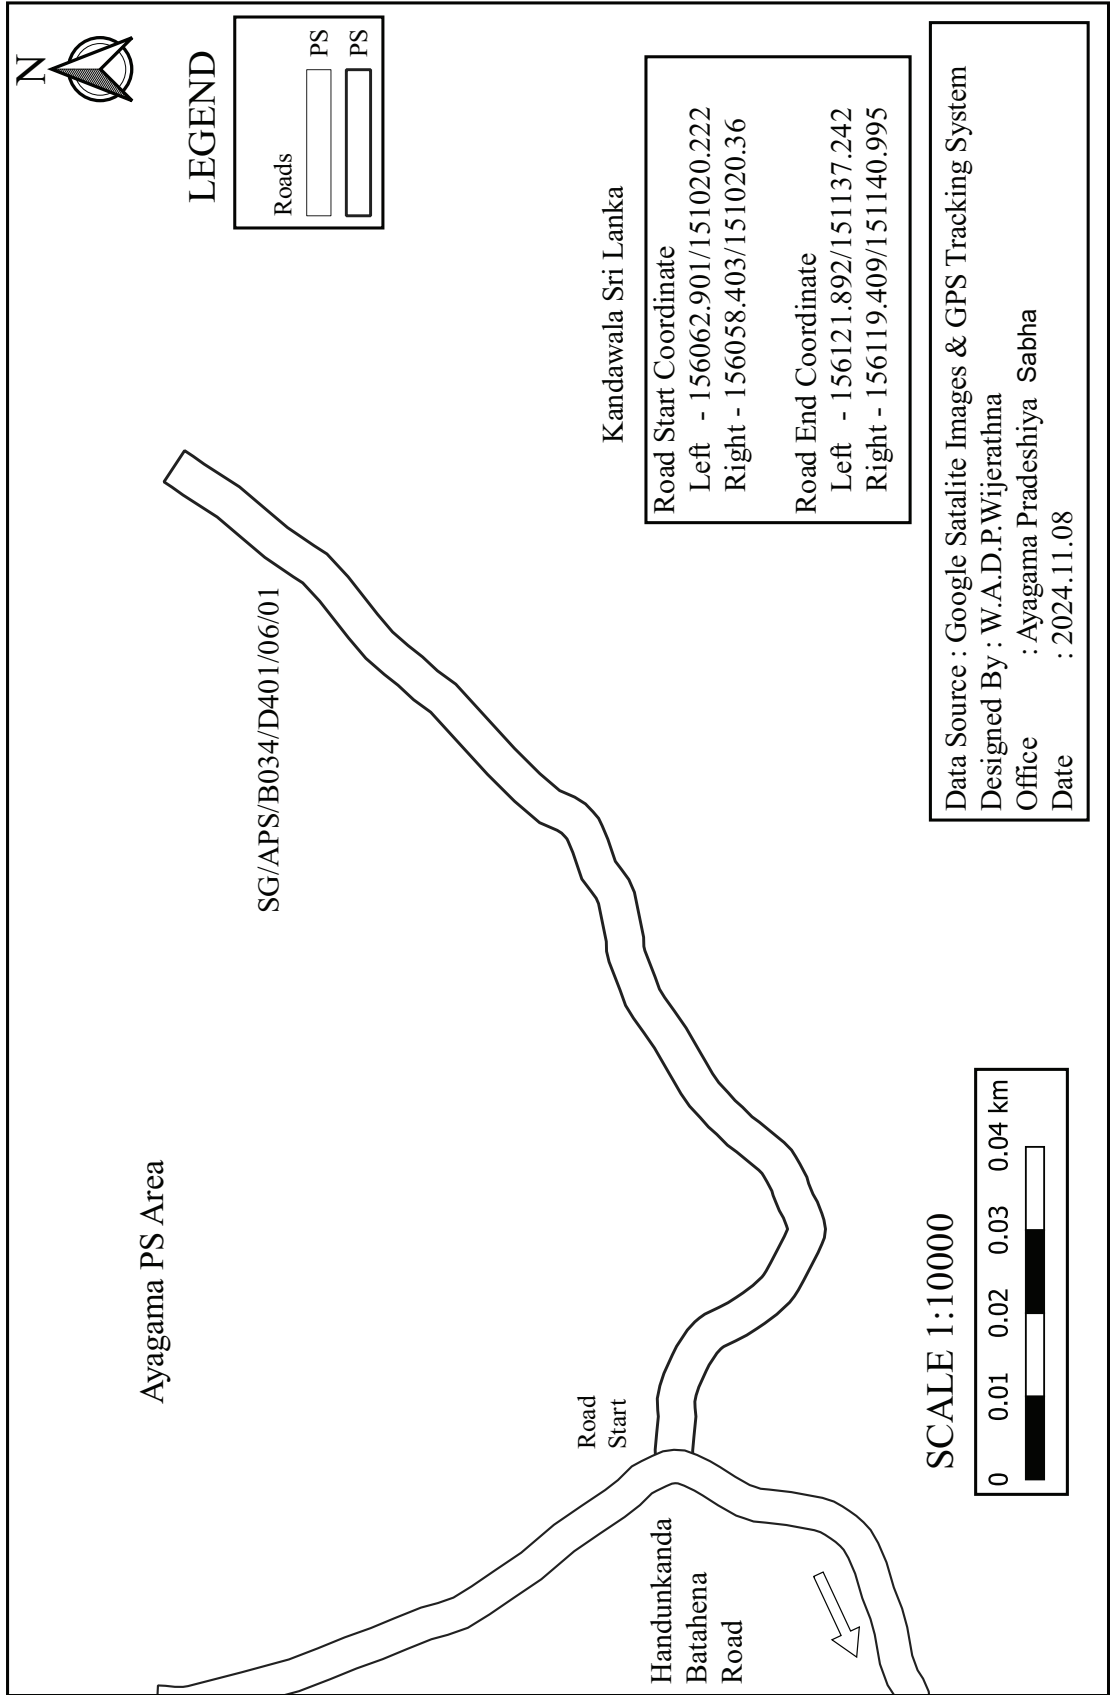

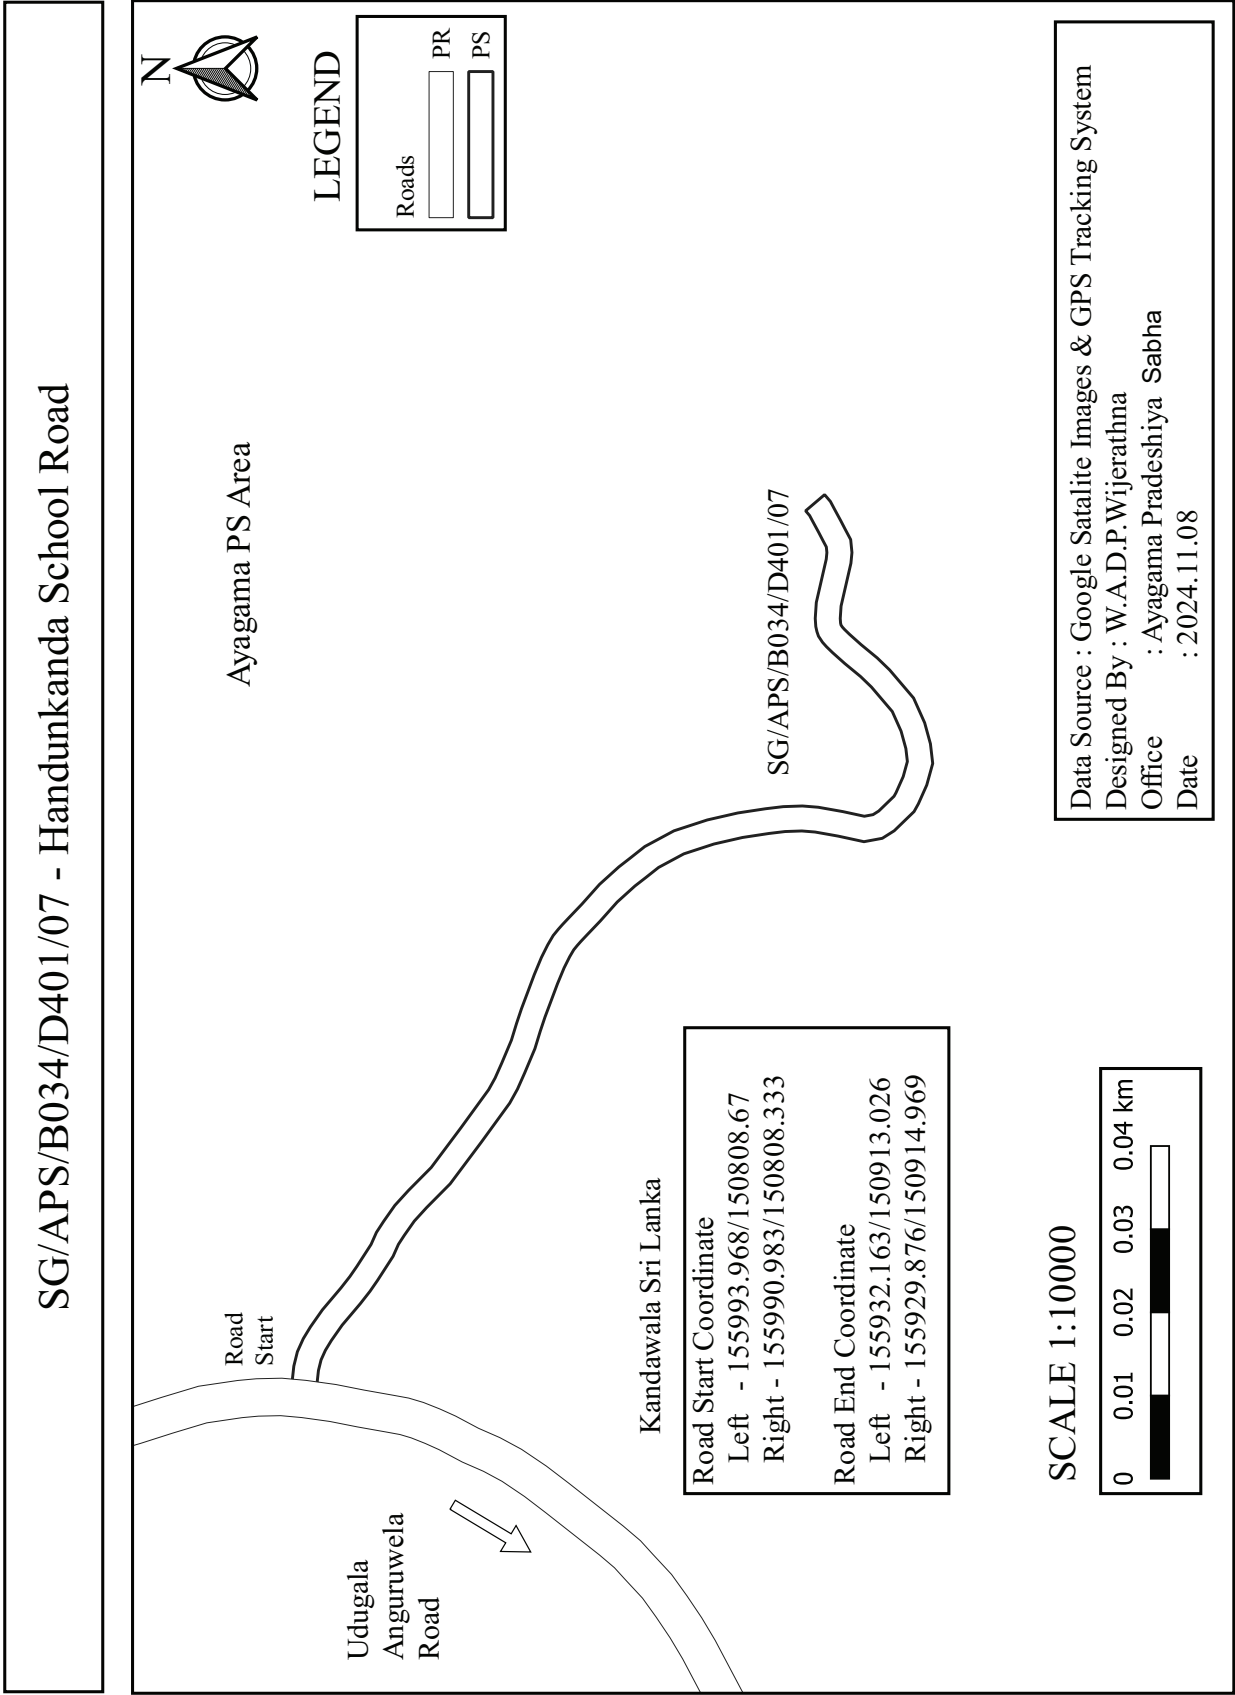



SG/APS/B034/D401/08 - First Lane of Handunkanda

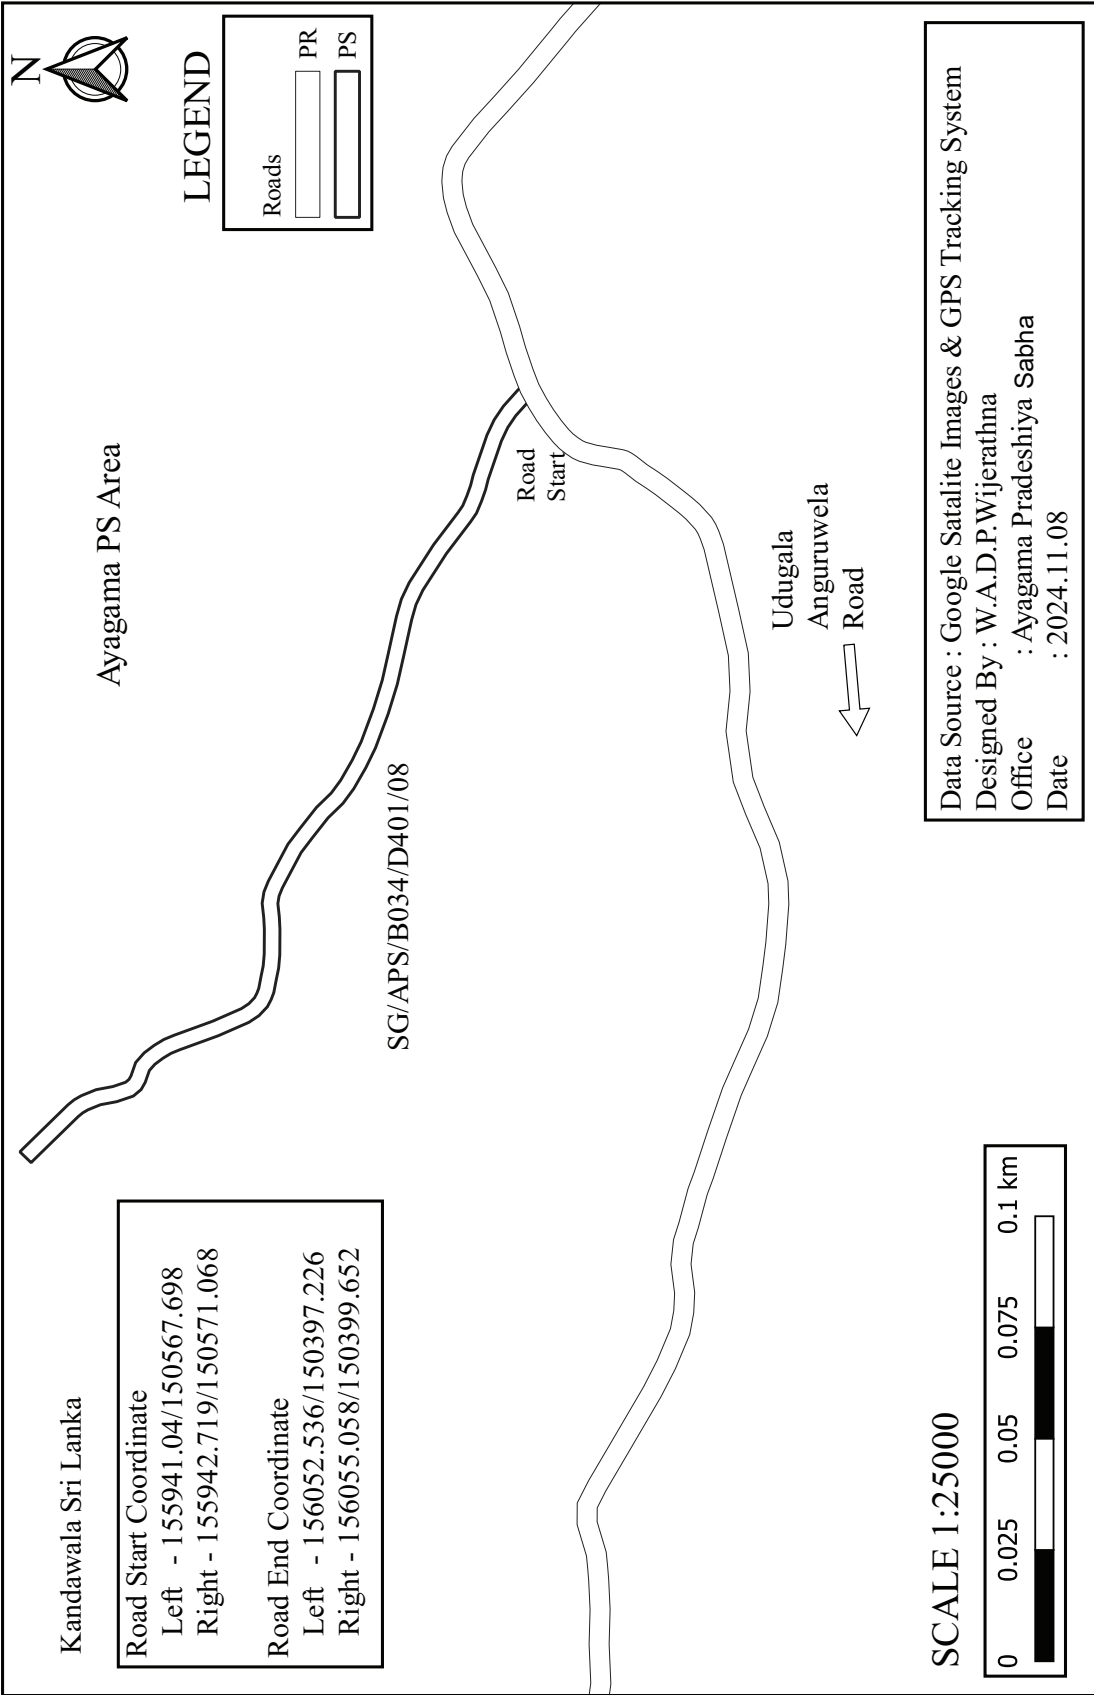

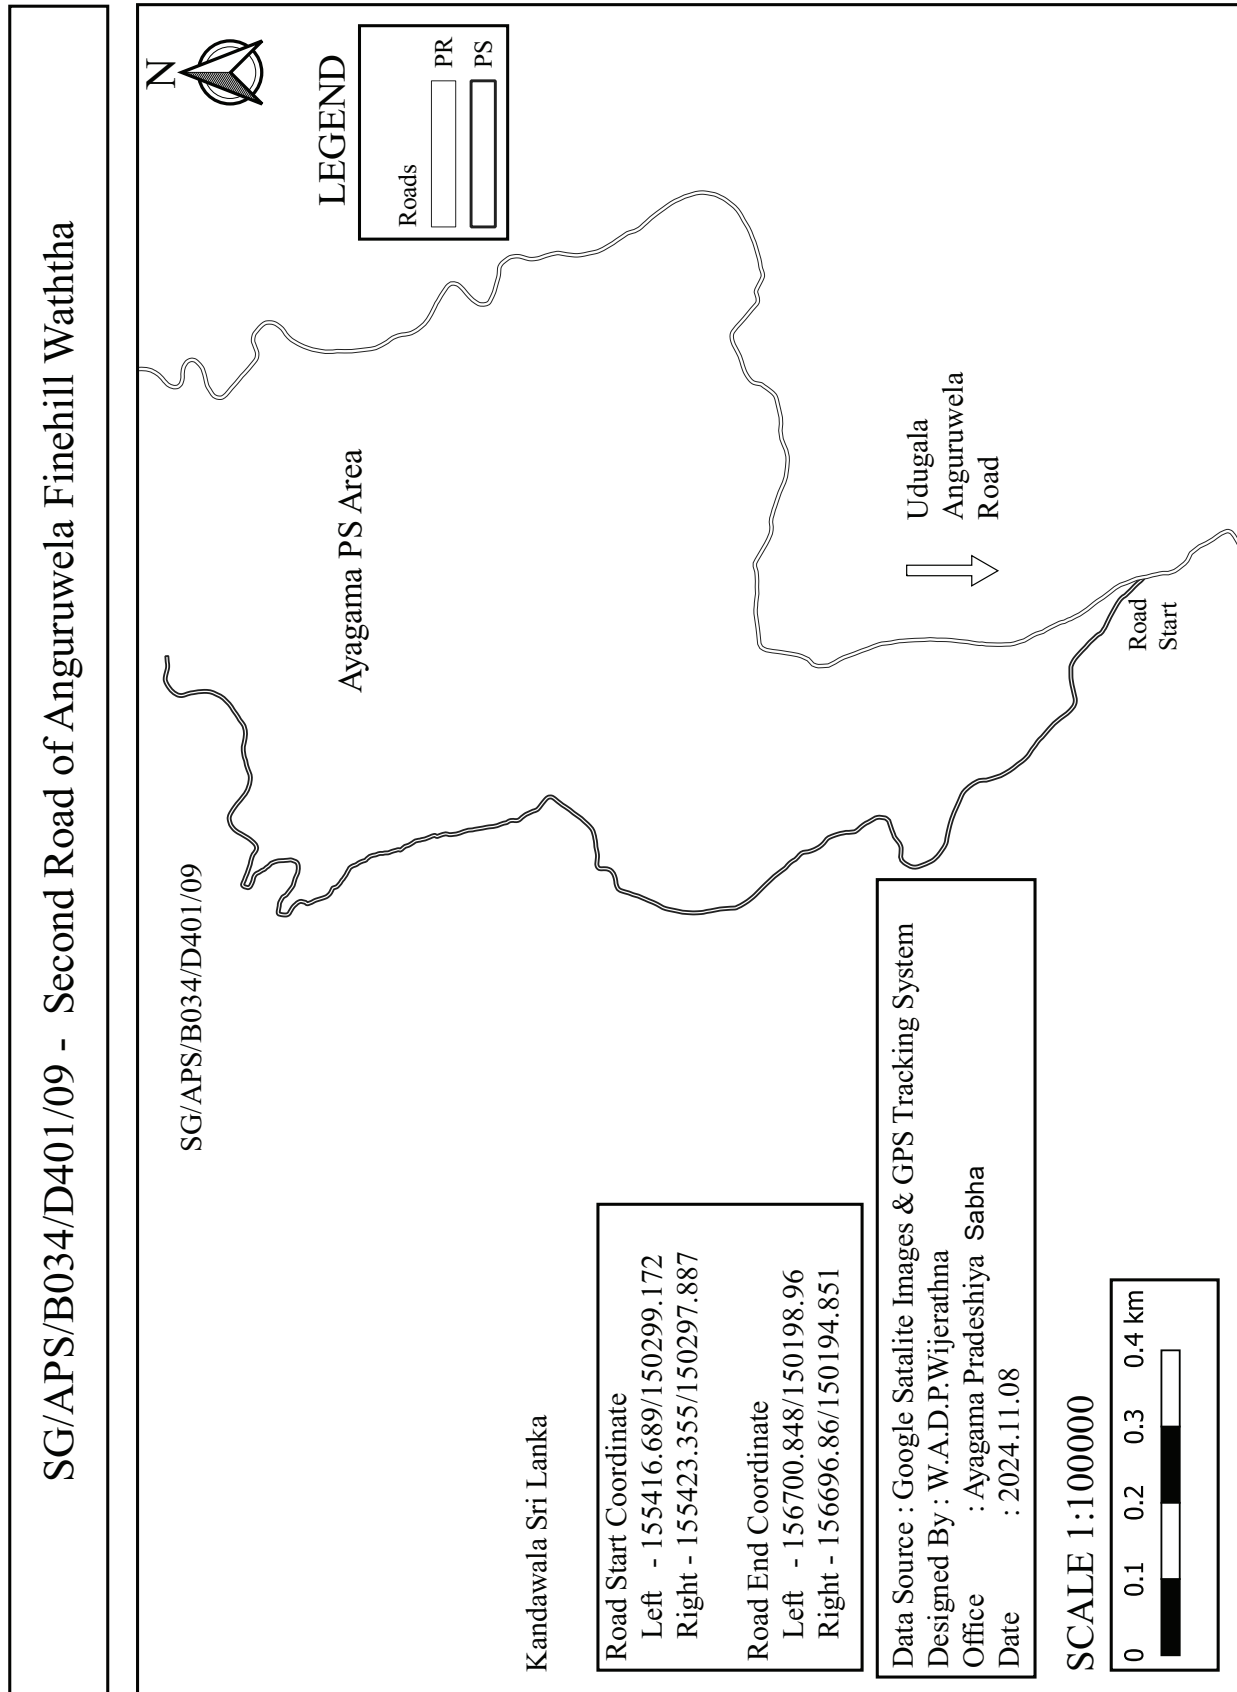



SG/APS/B034/D401/10 - Fourth Lane of Udugala Anguruwela Road

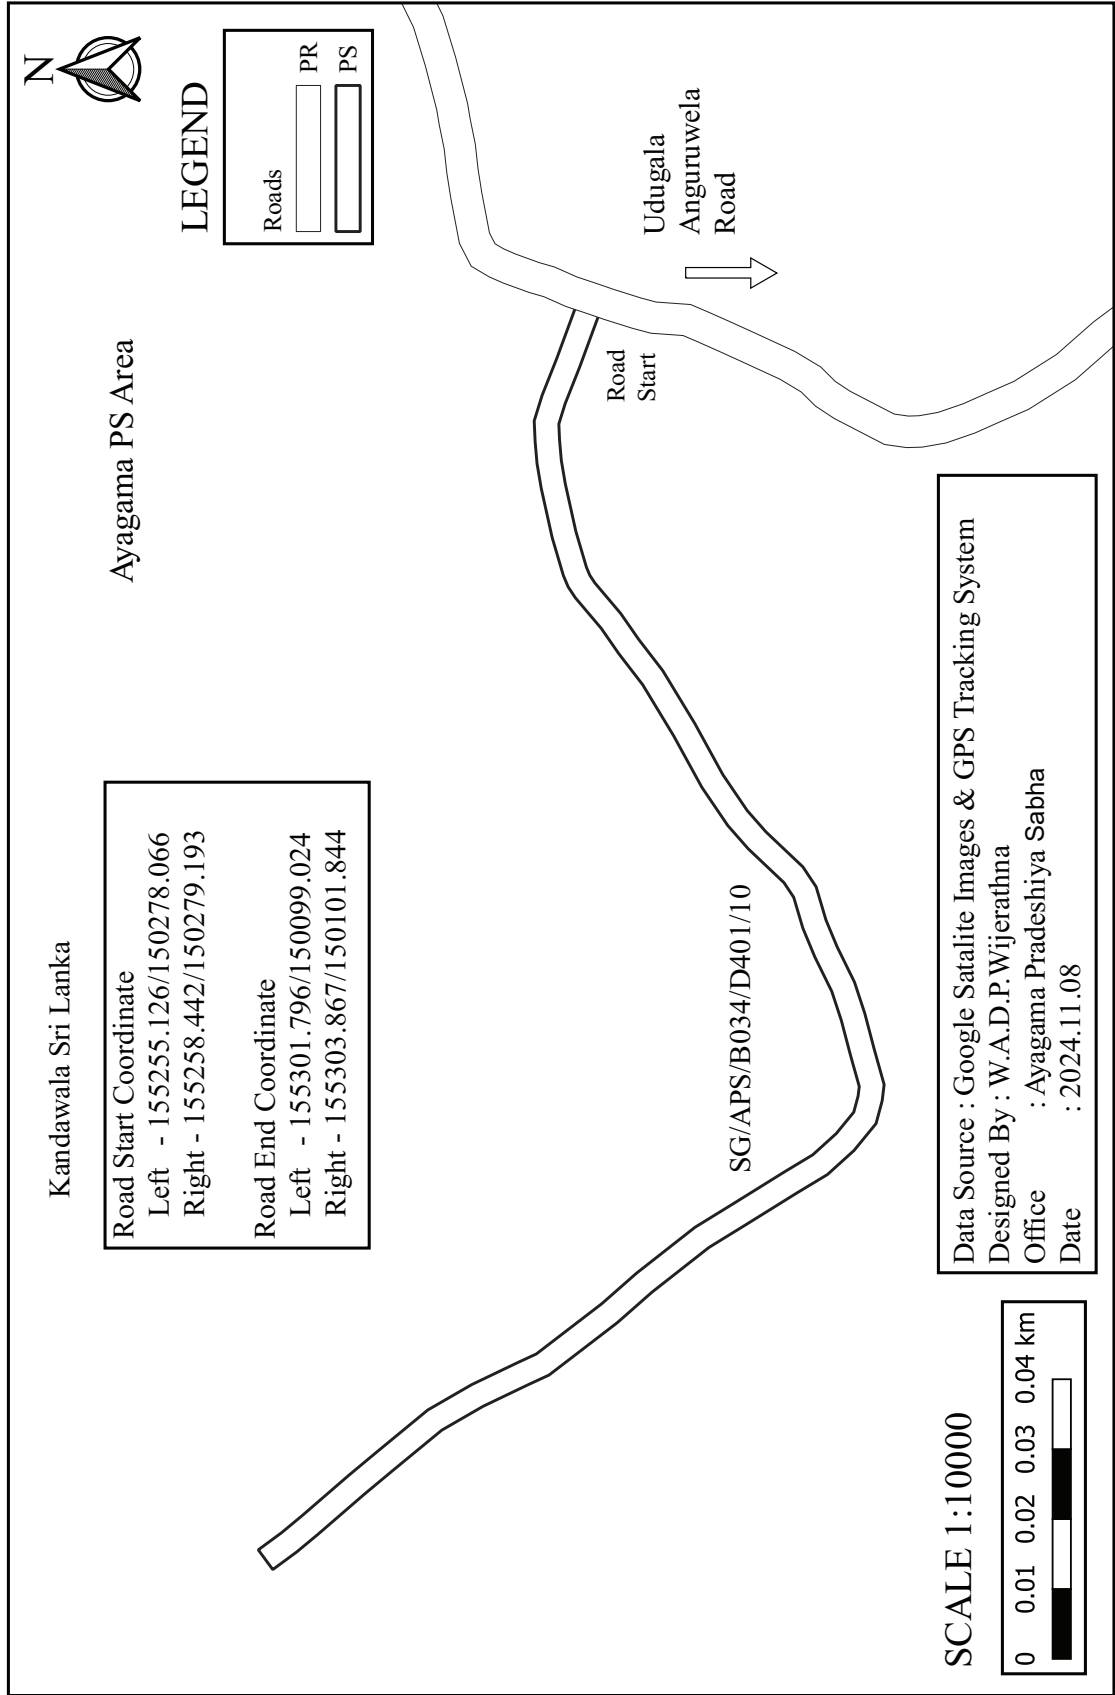


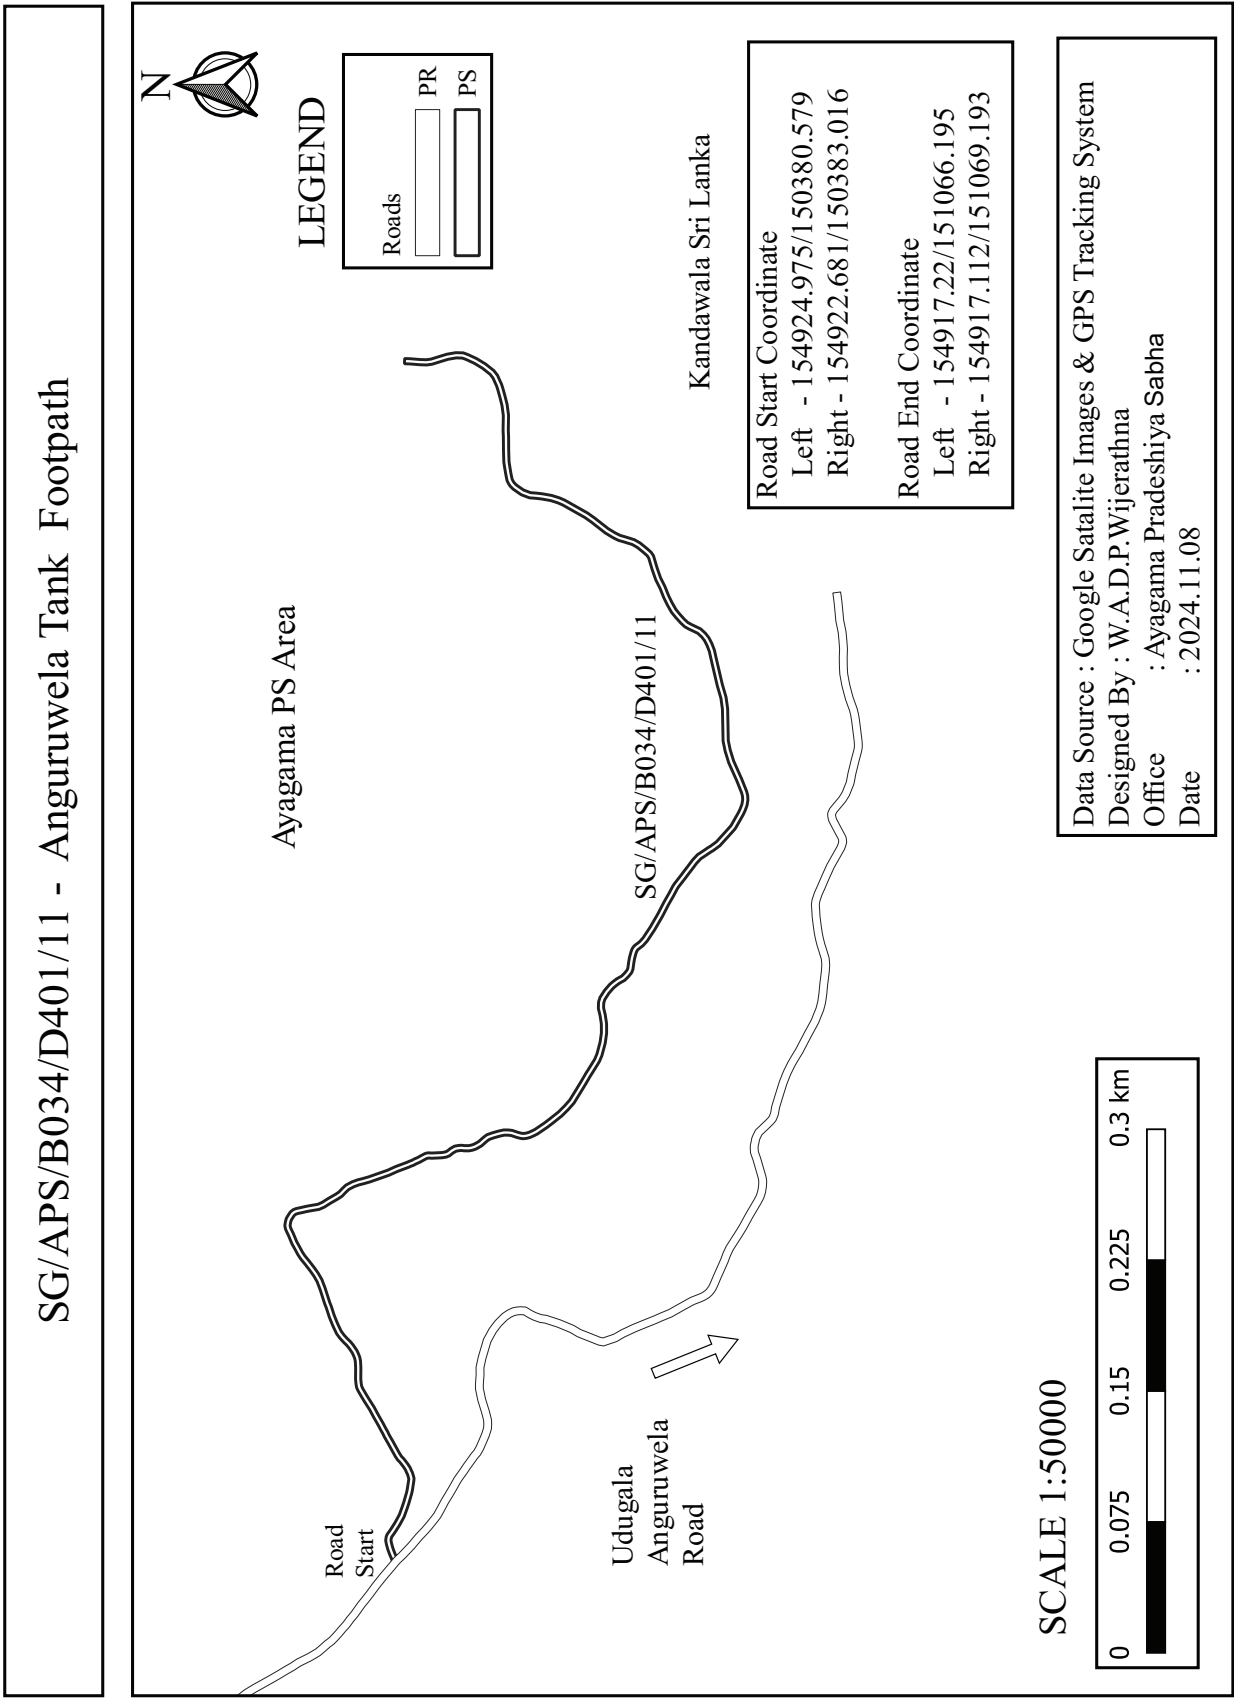

SG/APS/B034/D401/12 - First Lane of Panwilahena

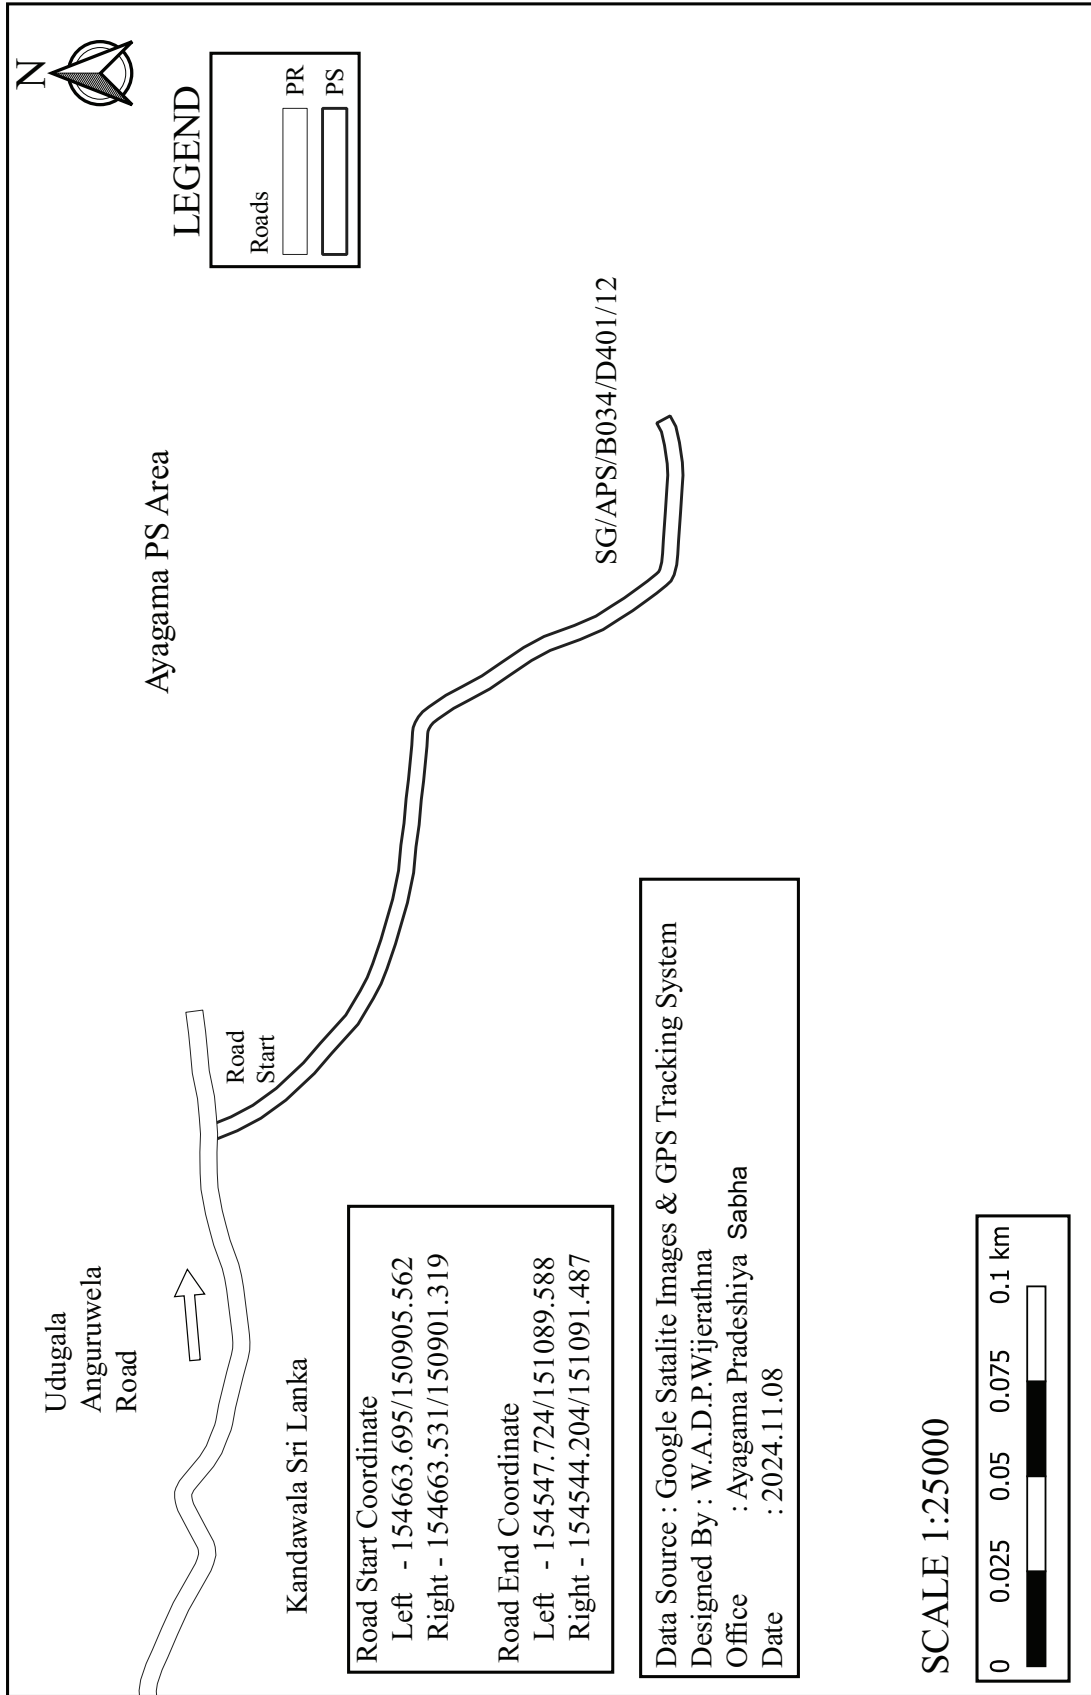

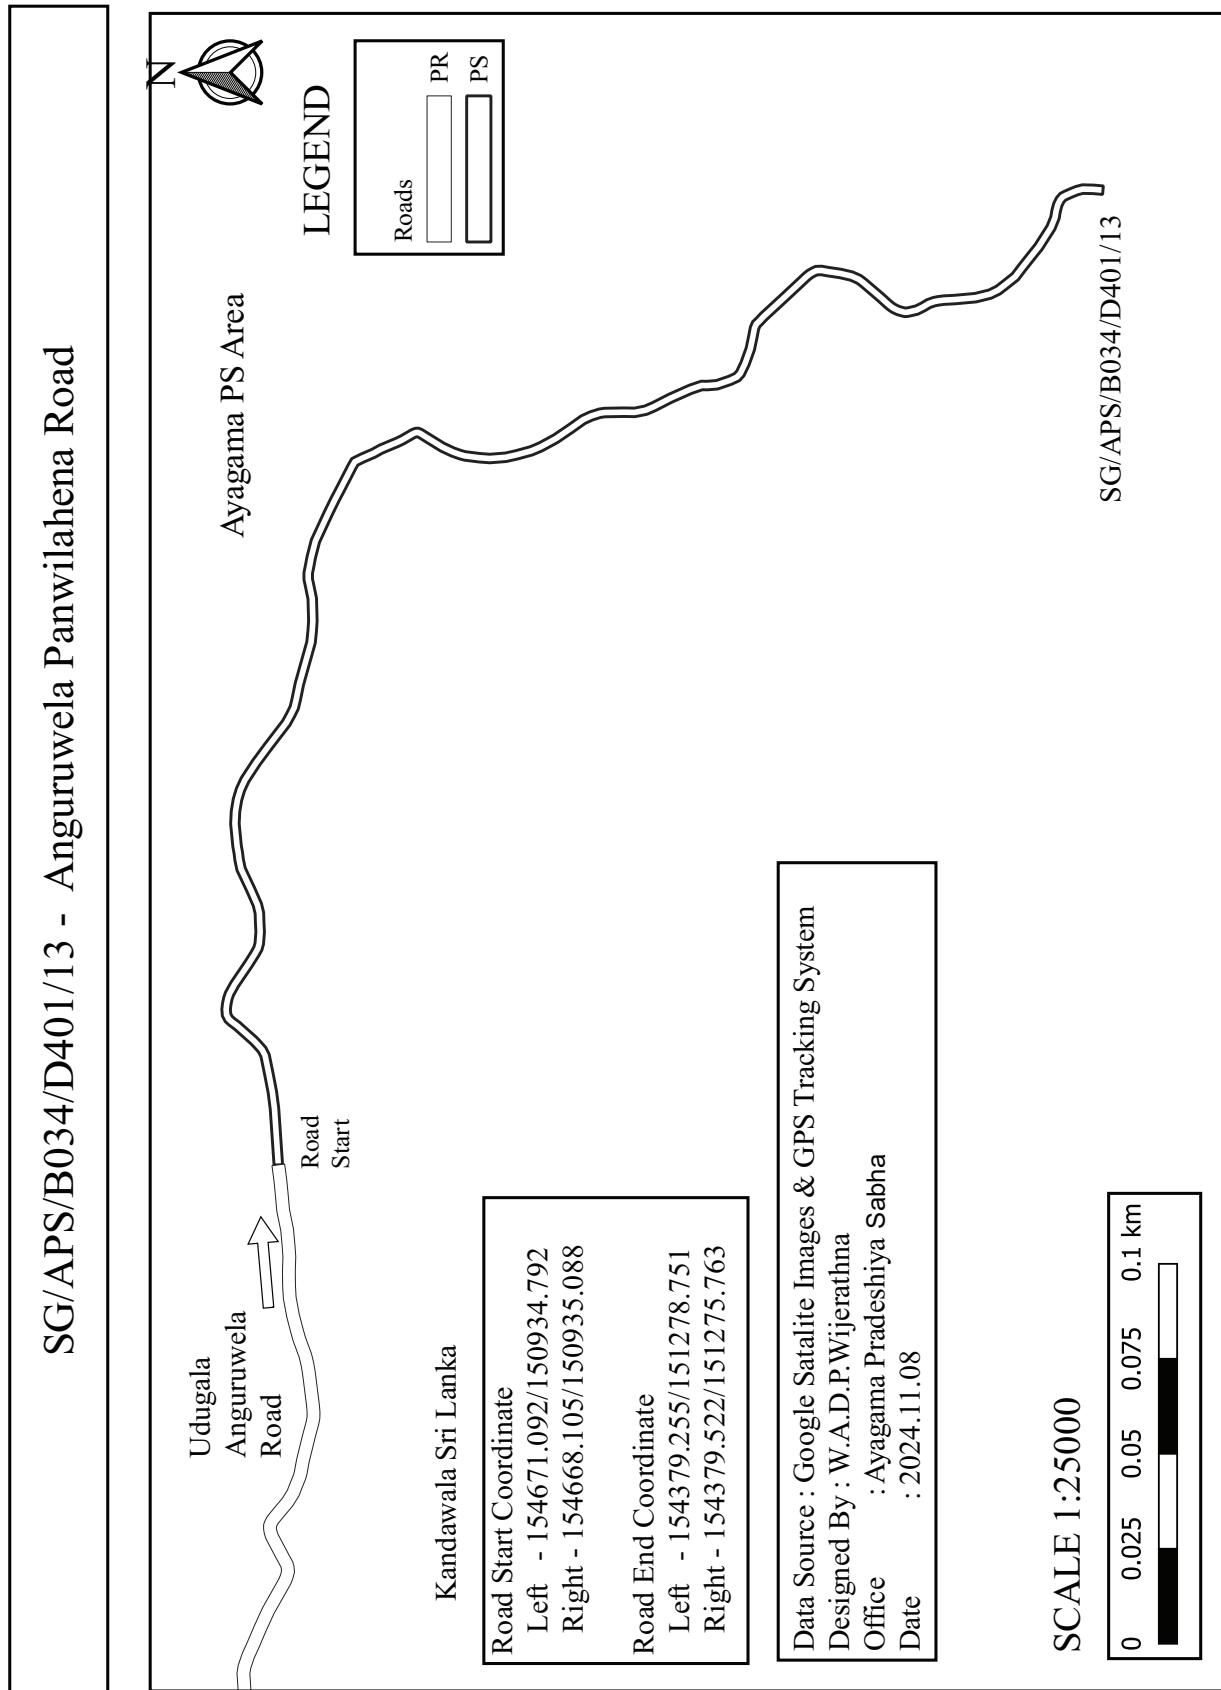

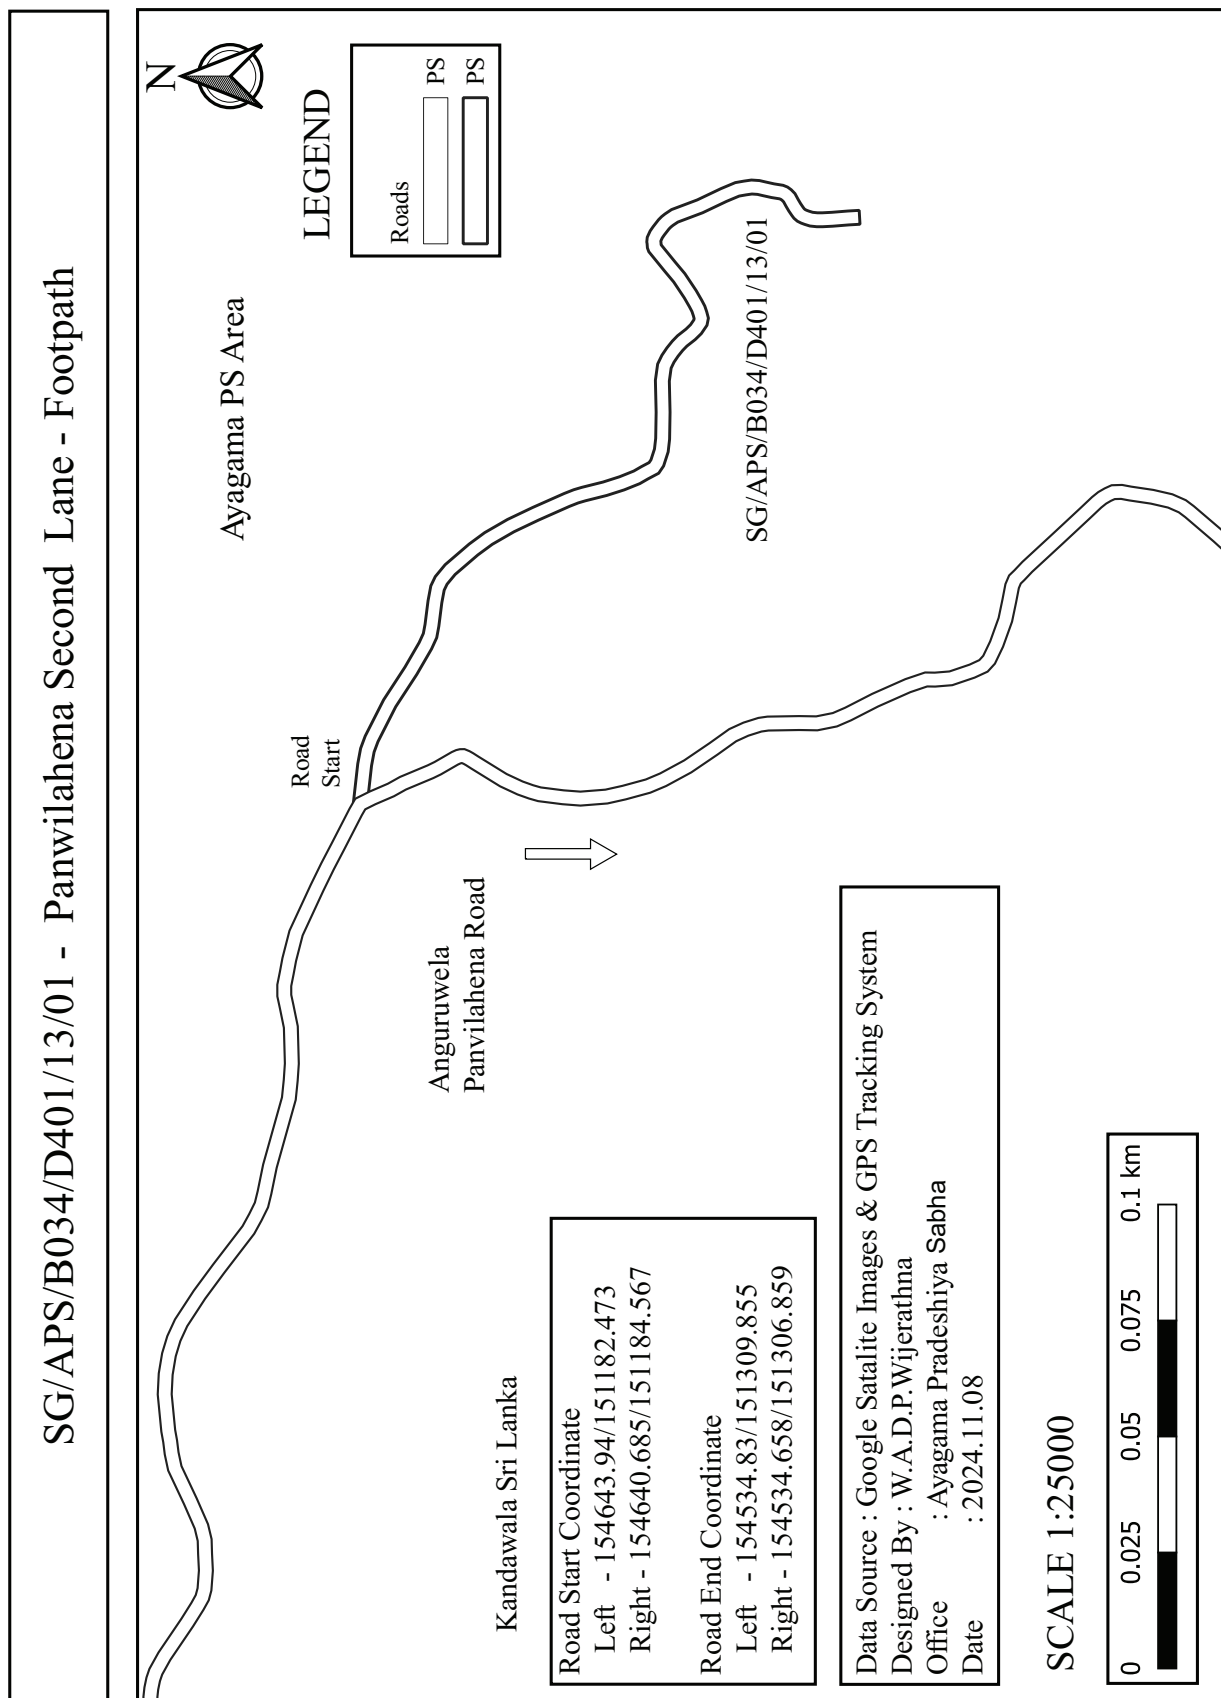

The figure is a map of the Ayagama PS Area, showing a network of roads. The map includes a legend, a scale bar, and a north arrow. The legend indicates that the roads are categorized by color: red for RDA, orange for PR, and yellow for PS. The scale bar shows a distance of 0.4 km. The north arrow points towards the top right. The map also includes a title block with the following information:

Kandawala Sri Lanka

Road Start Coordinate
Left - 153527.299/154057.44
Right - 153527.251/154061.441

Road End Coordinate
Left - 154282.721/153664.727
Right - 154279.844/153667.505

Data Source : Google Satalite Images & GPS Tracking System
Designed By : W.A.D.P.Wijerathna
Office : Ayagama Pradeshiya Sabha
Date : 2024.11.08

SG/APS/B034/C403/01

Ayagama PS Area

SCALE 1:100000

0 0.1 0.2 0.3 0.4 km

Road Start


Pimbura Karawita Road

SG/APS/B034/C403/02 - Kukuluwa Rajamaha vihara First Mawatha

Data Source : Google Satalite Images & GPS Tracking System
 Designed By : W.A.D.P.Wijerathna
 Office : Ayagama Pradeshiya Sabha
 Date : 2024.11.08

Kandawala Sri Lanka

Road Start Coordinate
 Left - 153415.092/154520.334
 Right - 153416.359/154526.083
 Road End Coordinate
 Left - 154548.876/155593.224
 Right - 154549.724/155596.62

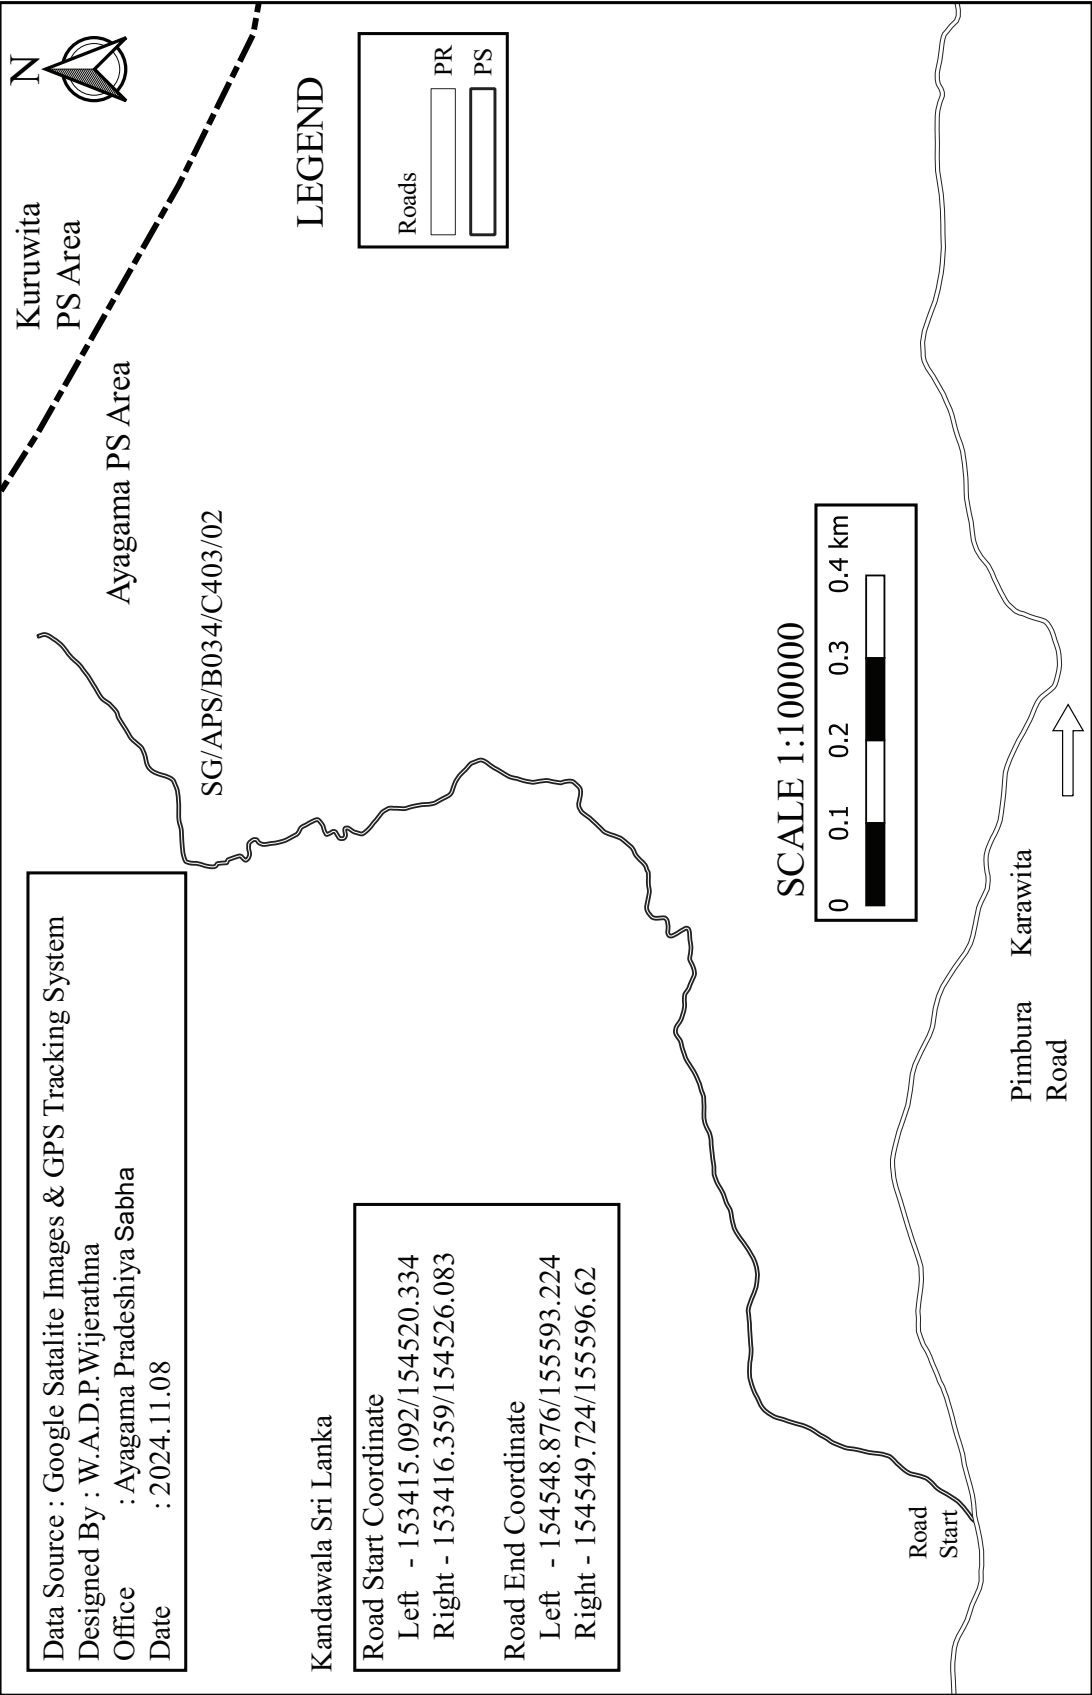



SG/APS/B034/C403/03 - Wellawaththa Nawinna Road

Data Source : Google Satalite Images & GPS Tracking System
 Designed By : W.A.D.P.Wijerathna
 Office : Ayagama Pradeshiya Sabha
 Date : 2024.11.08




Ayagama PS Area

Road
Start

Pimbura Road
 Karawita


LEGEND

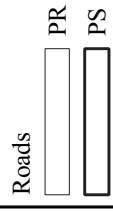


Kandawala Sri Lanka

Road Start Coordinate
 Left - 153491.897/154877.567
 Right - 153490.694/154874.125
 Road End Coordinate
 Left - 153259.975/154932.132
 Right - 153257.195/154930.006


SCALE 1:25000

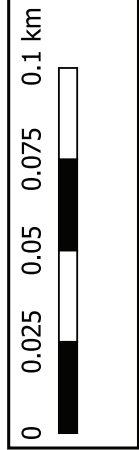


SG/APS/B034/C403/03

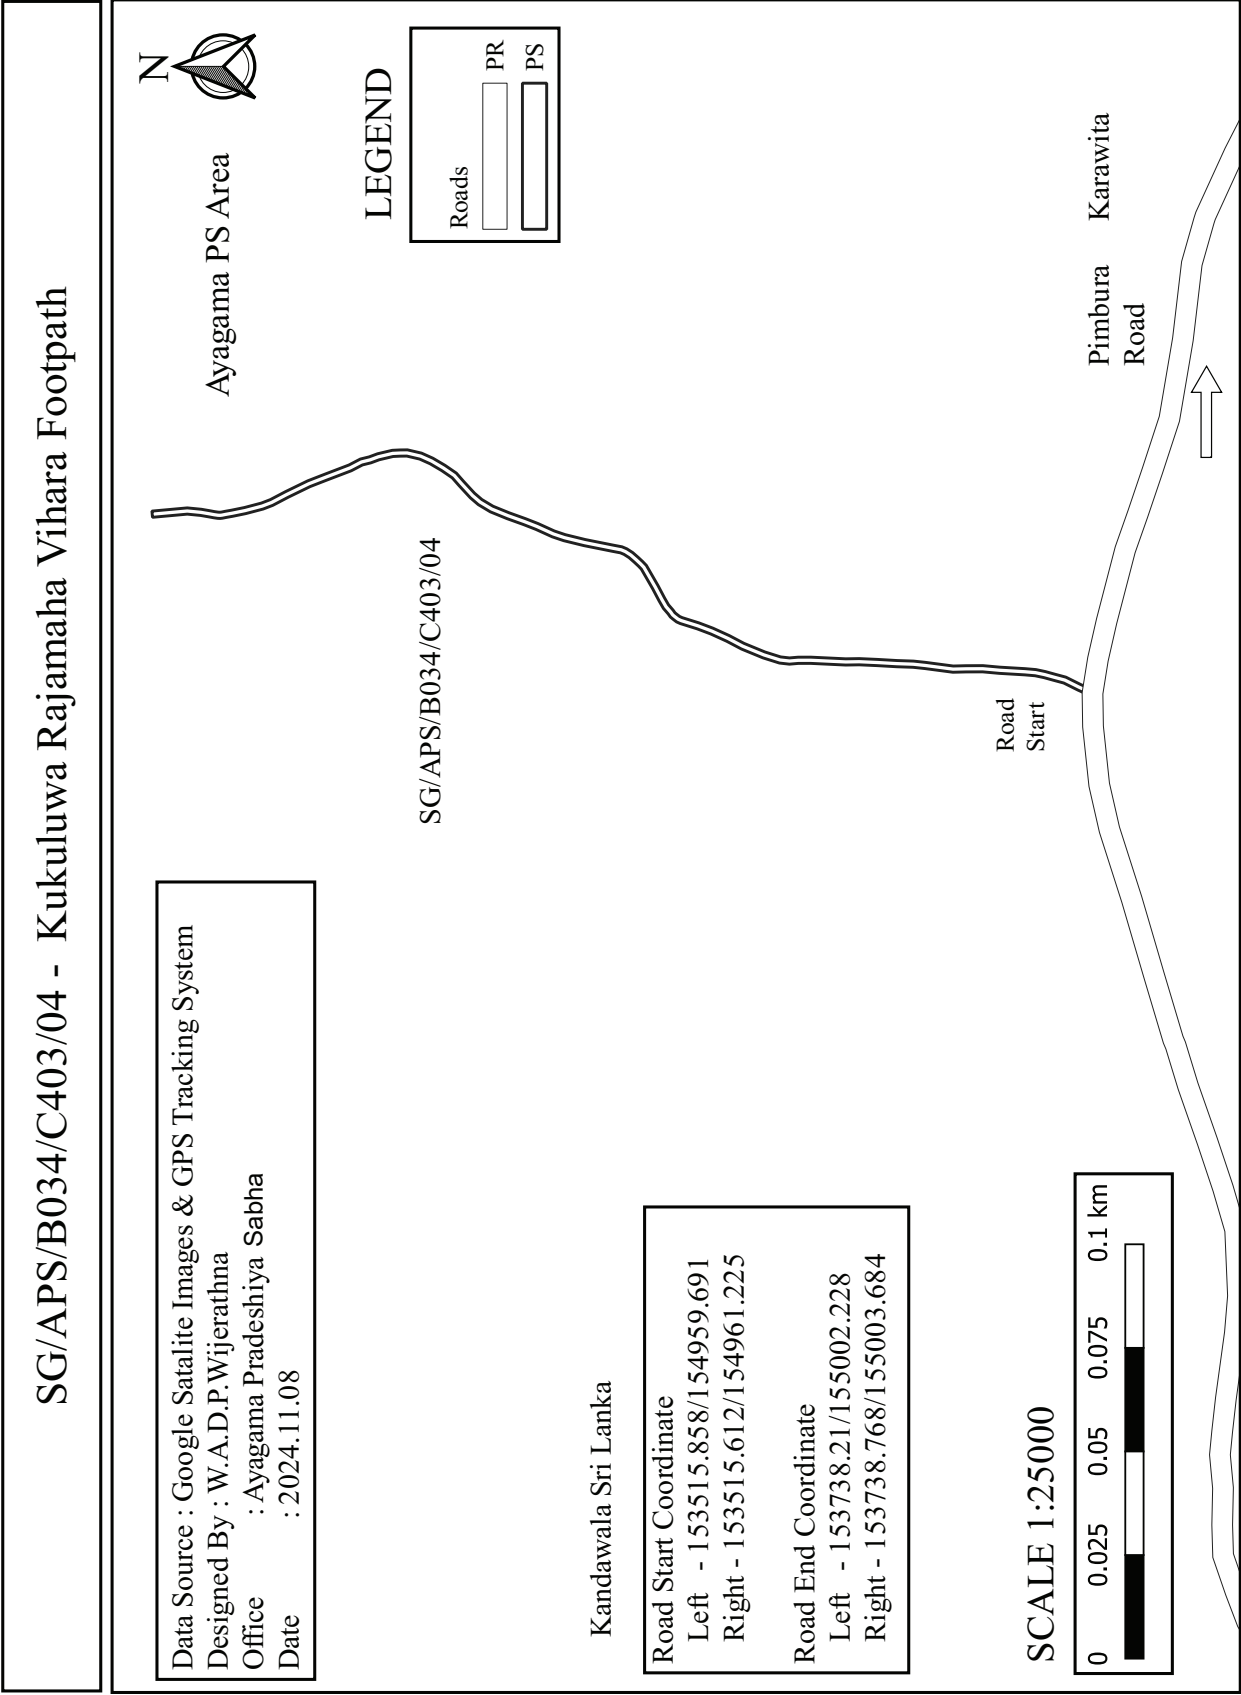



SG/APS/B034/C403/05 - Nawinnawaththa Dewala Road

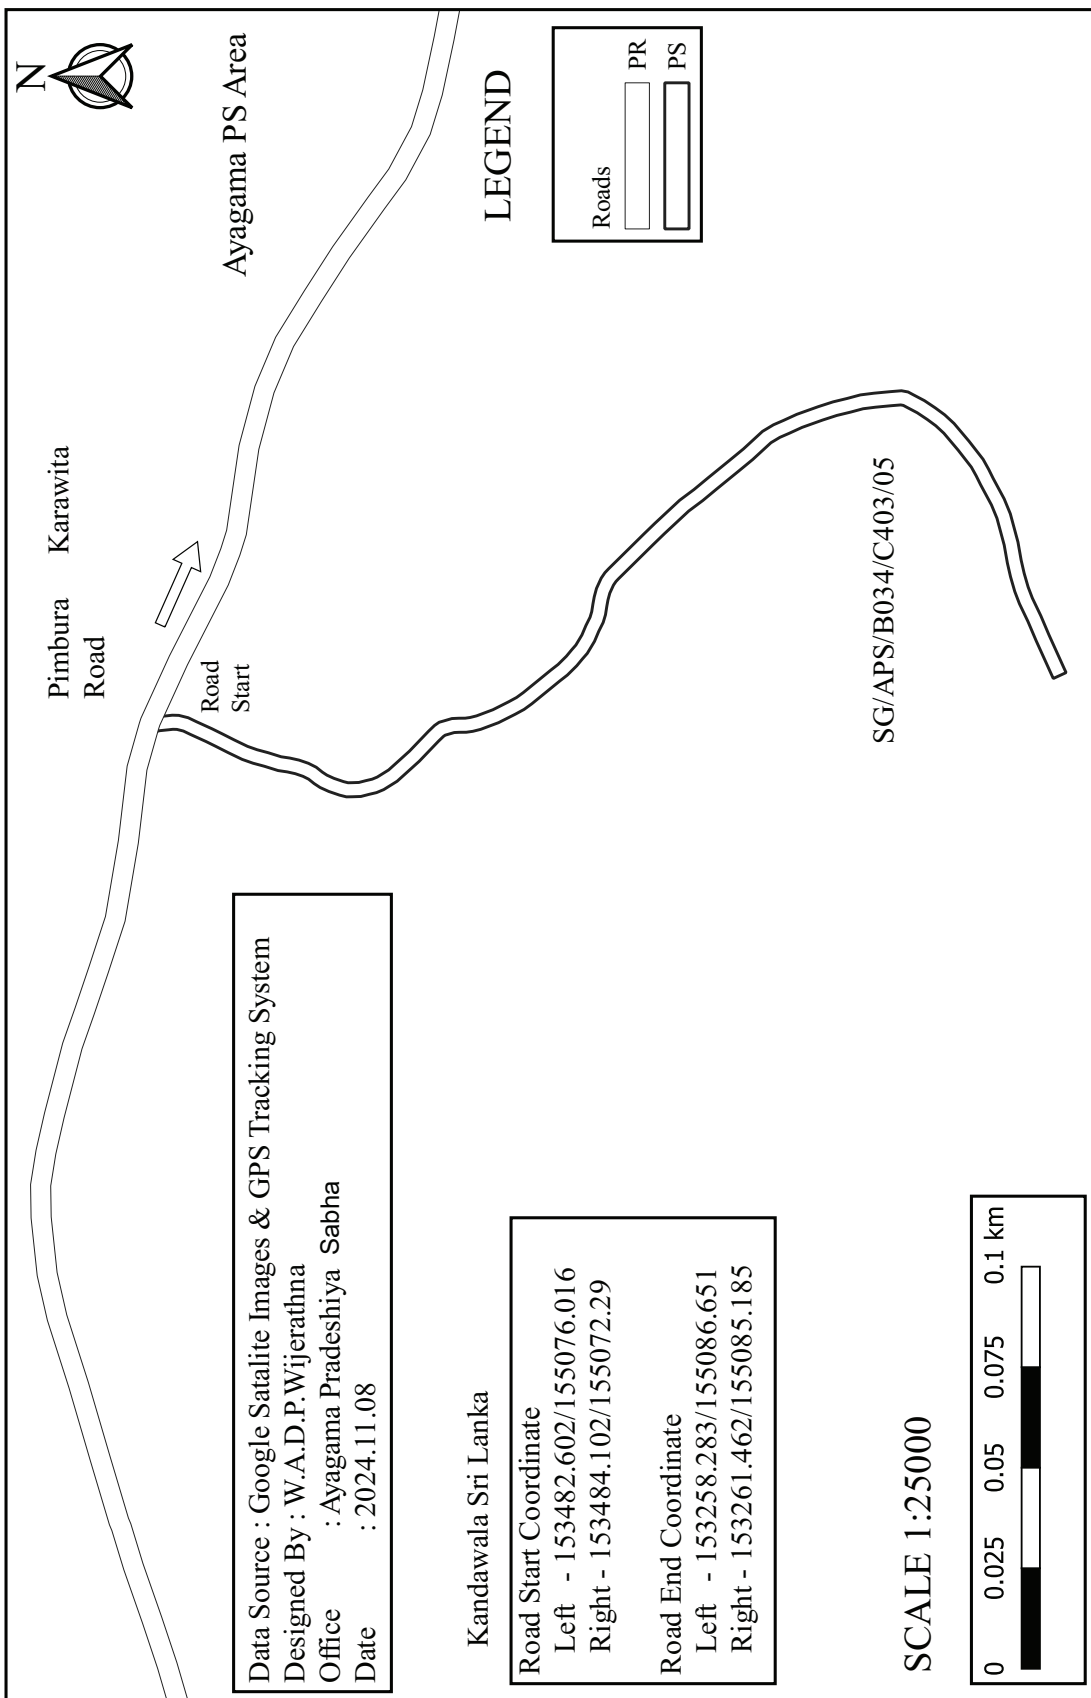

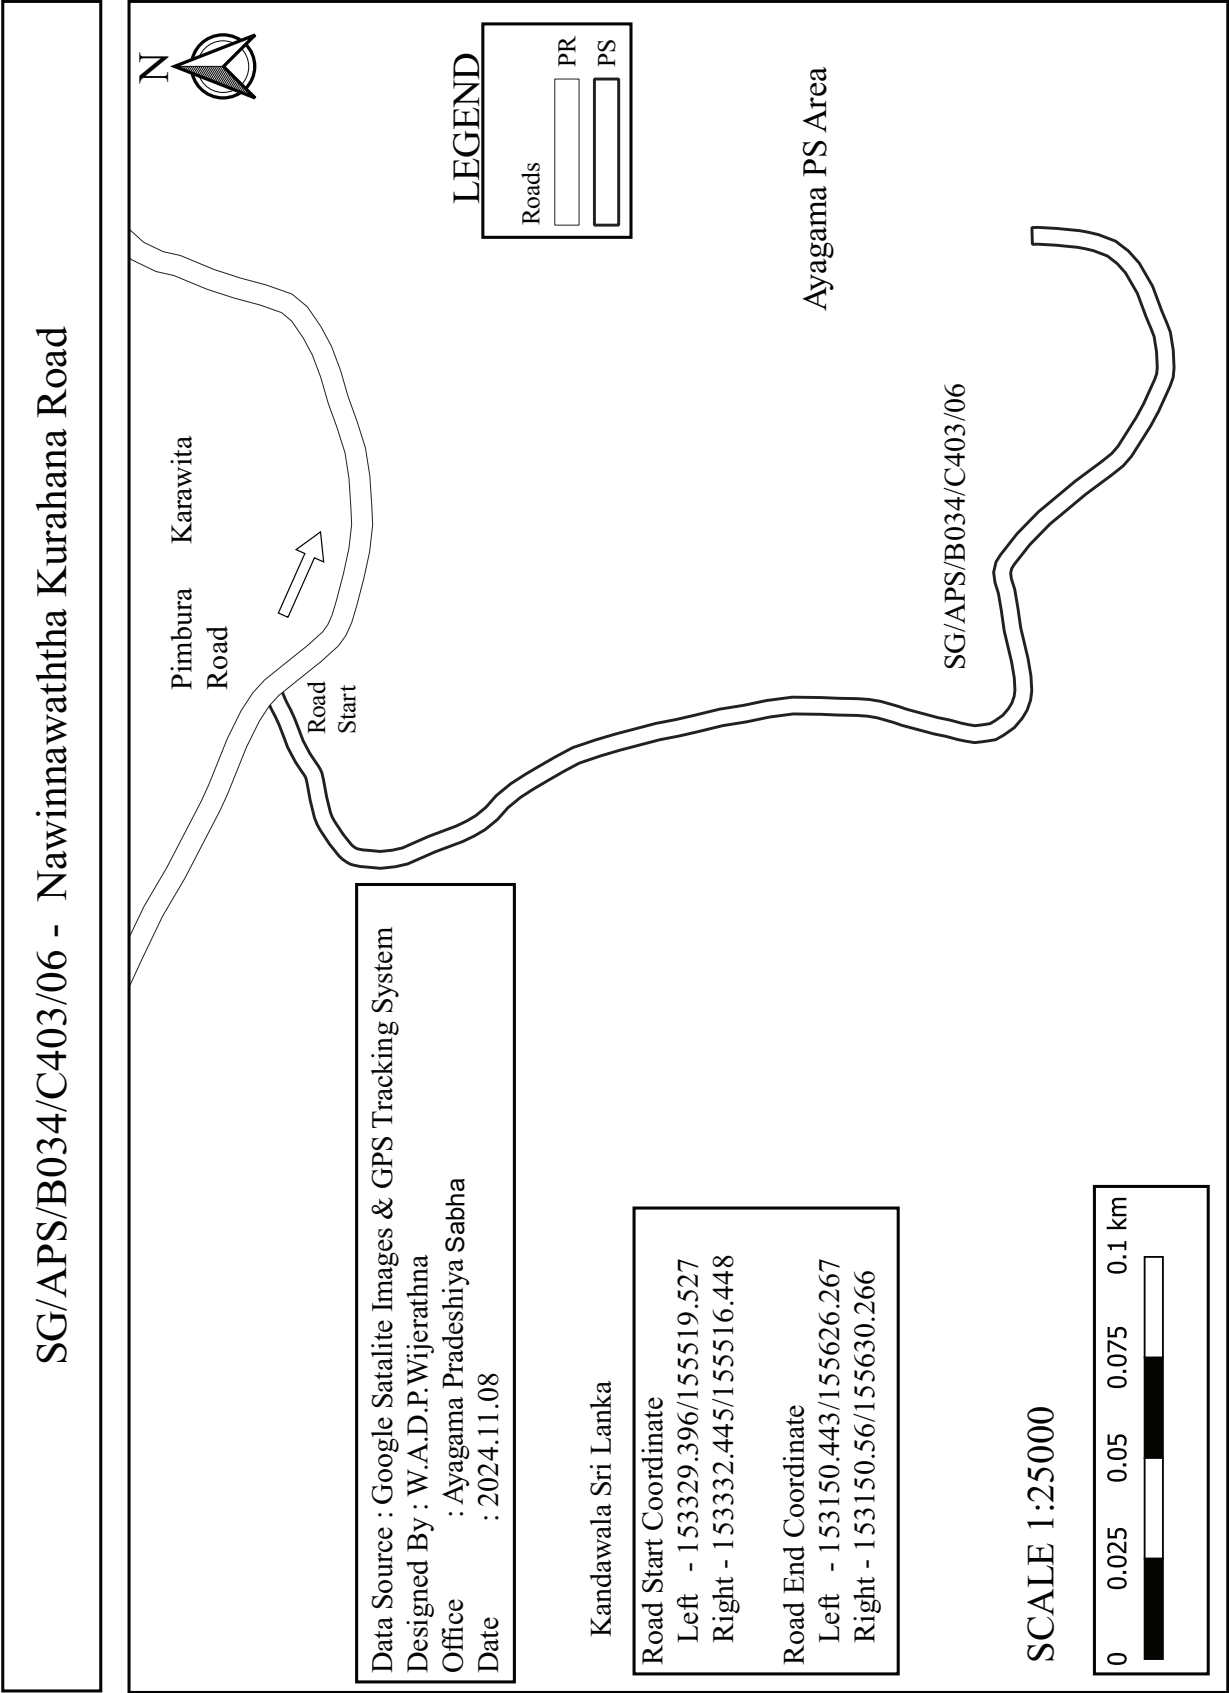


SG/APS/B034/C403/06/01 - Nawinnawaththa Madiththa Road

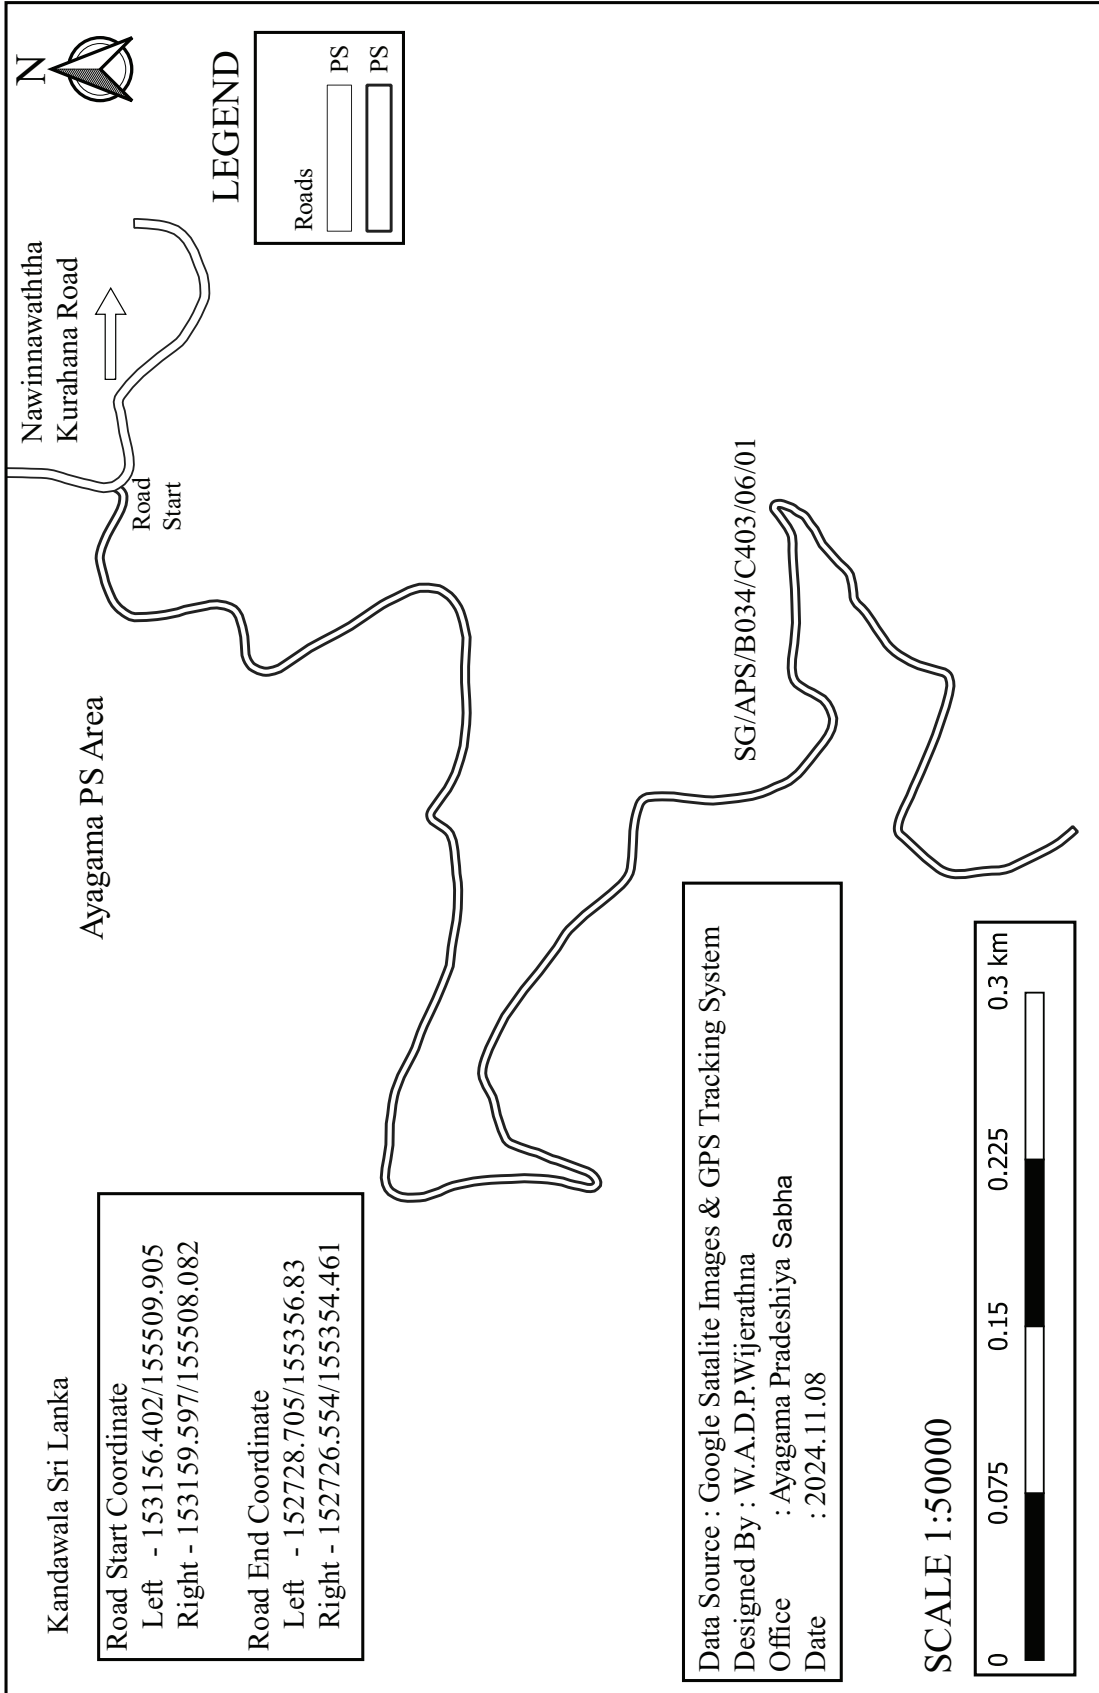


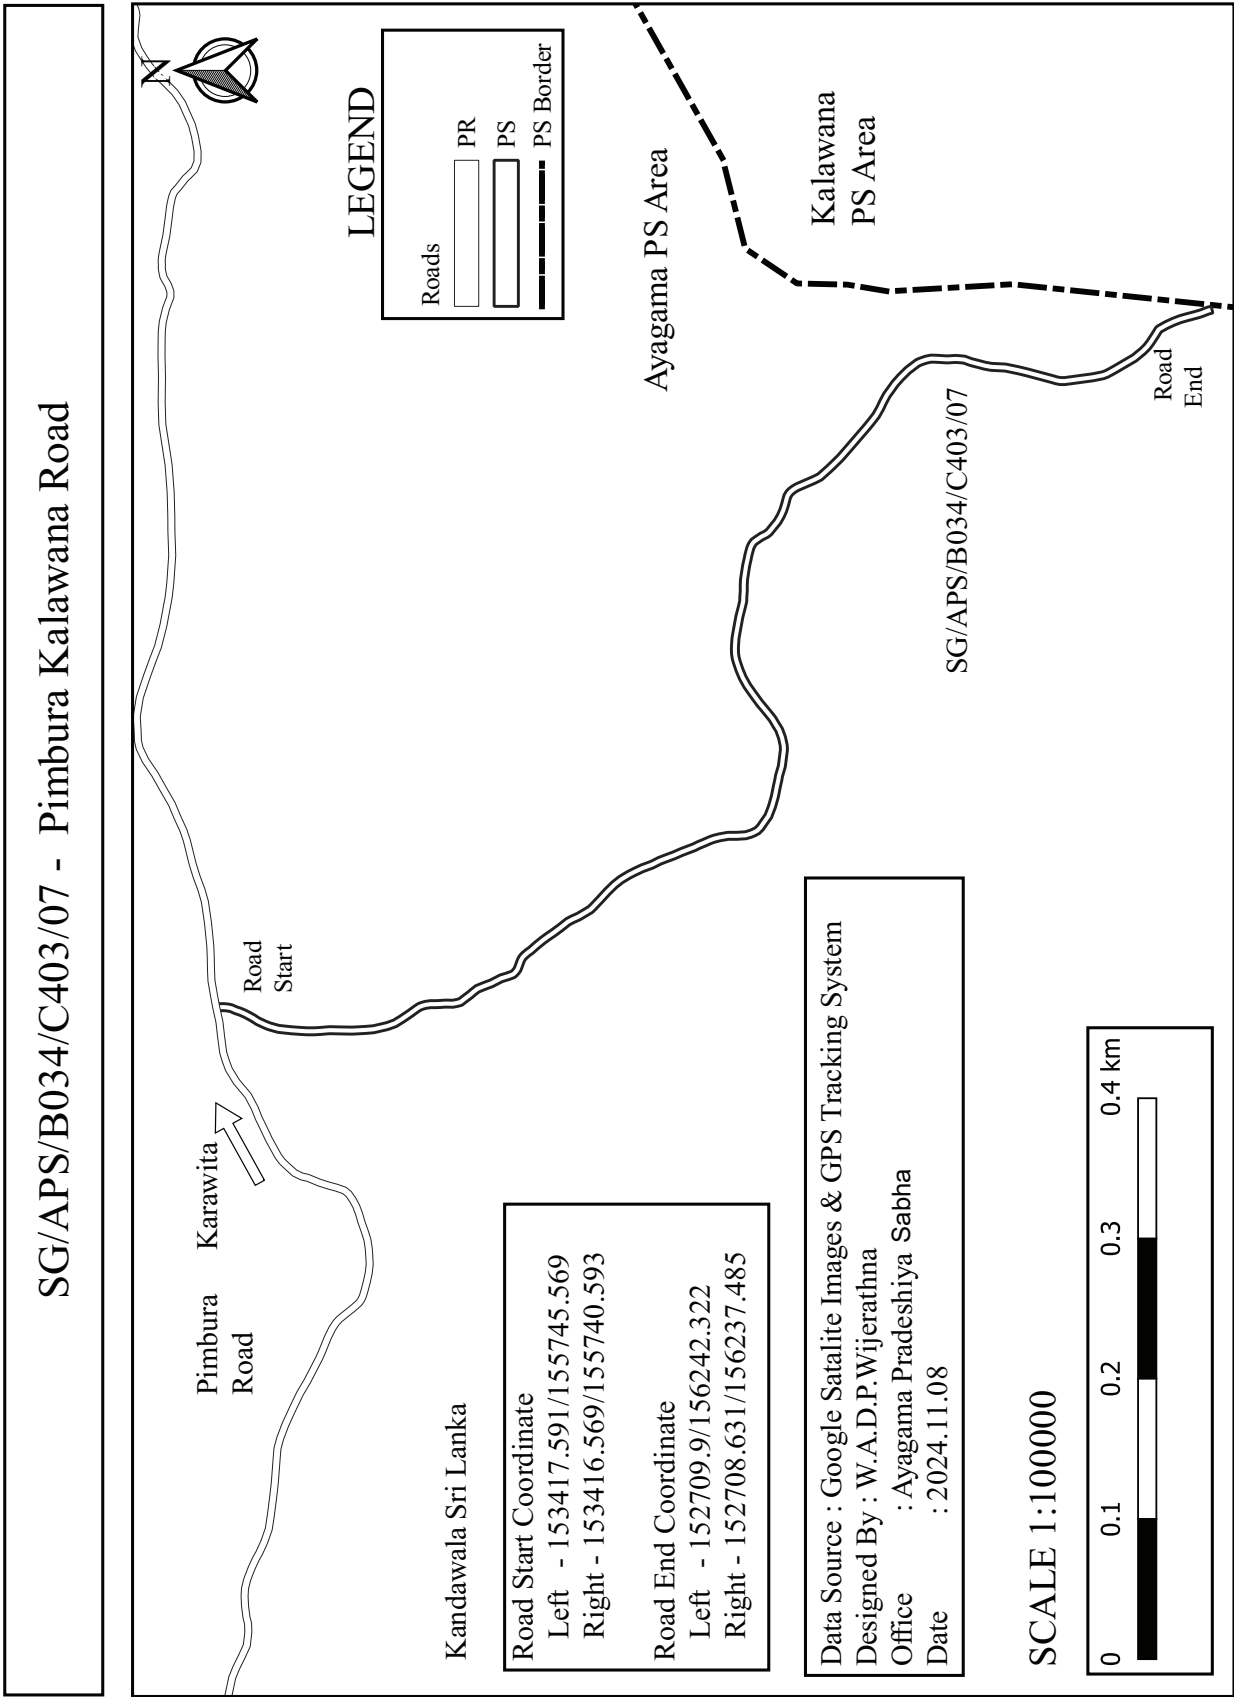

SG/APS/B034/C403/07/01 - Thennahena Road

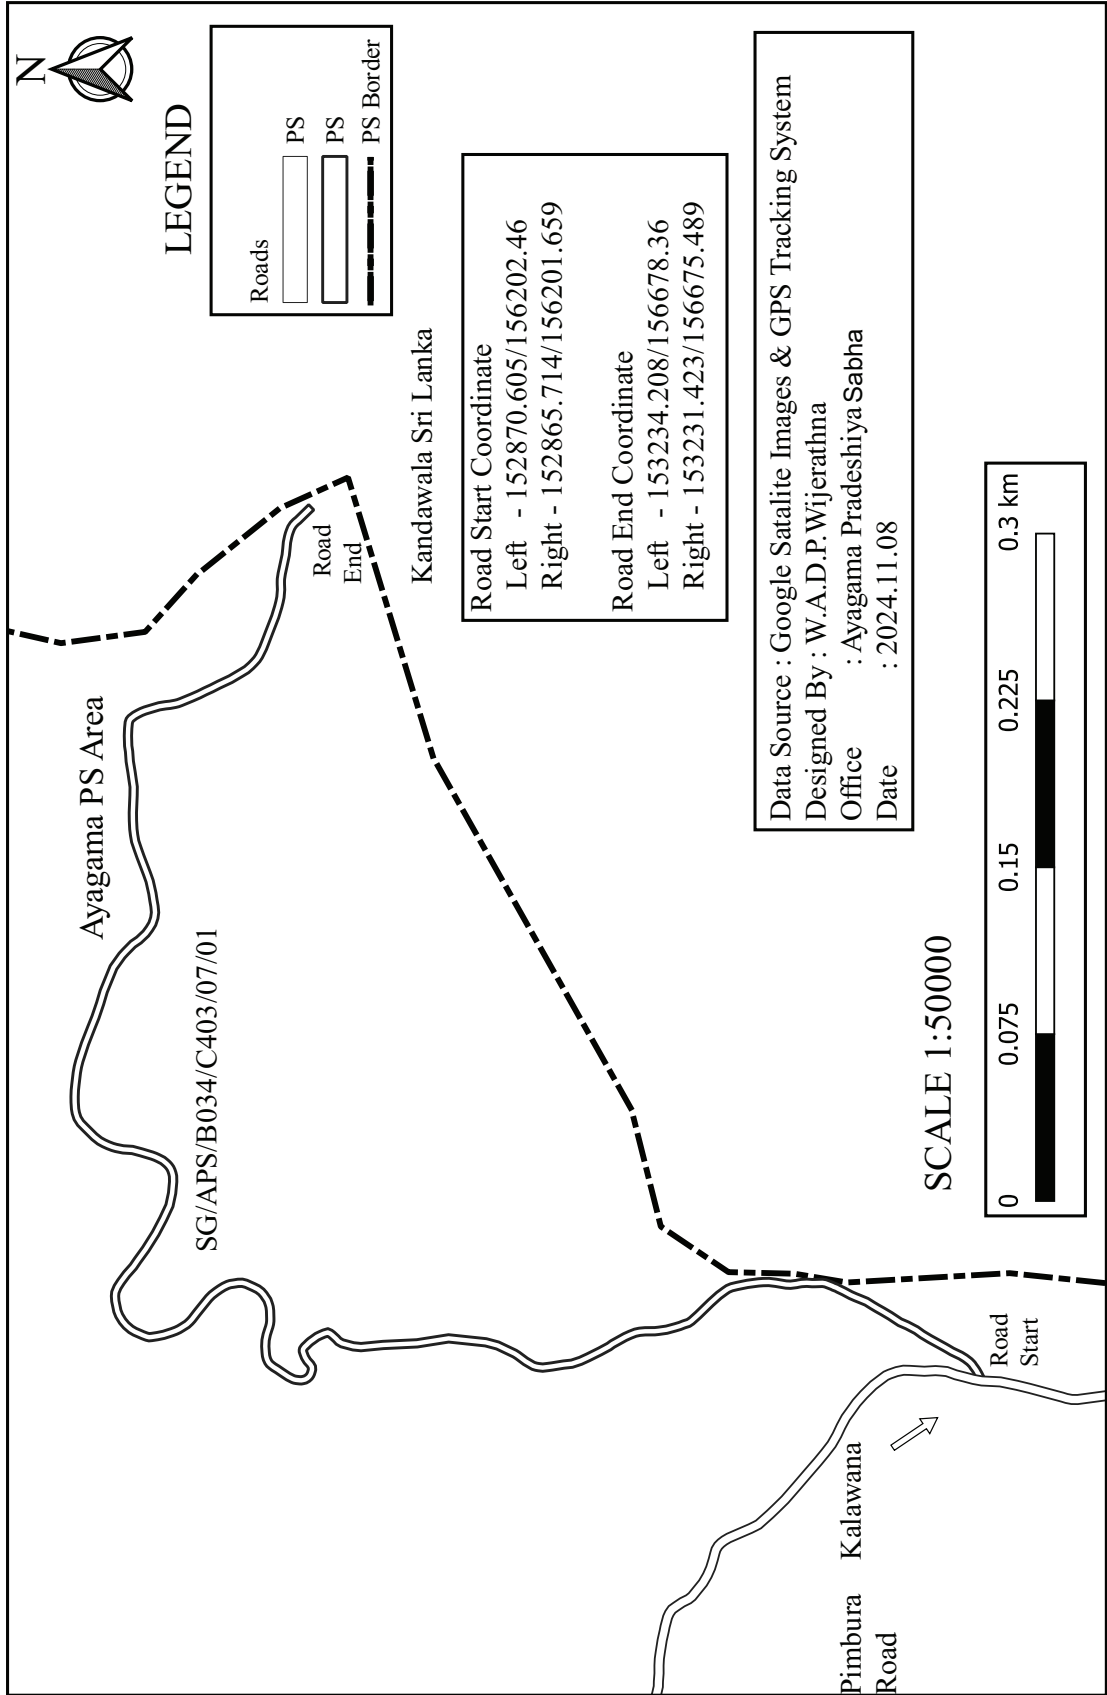



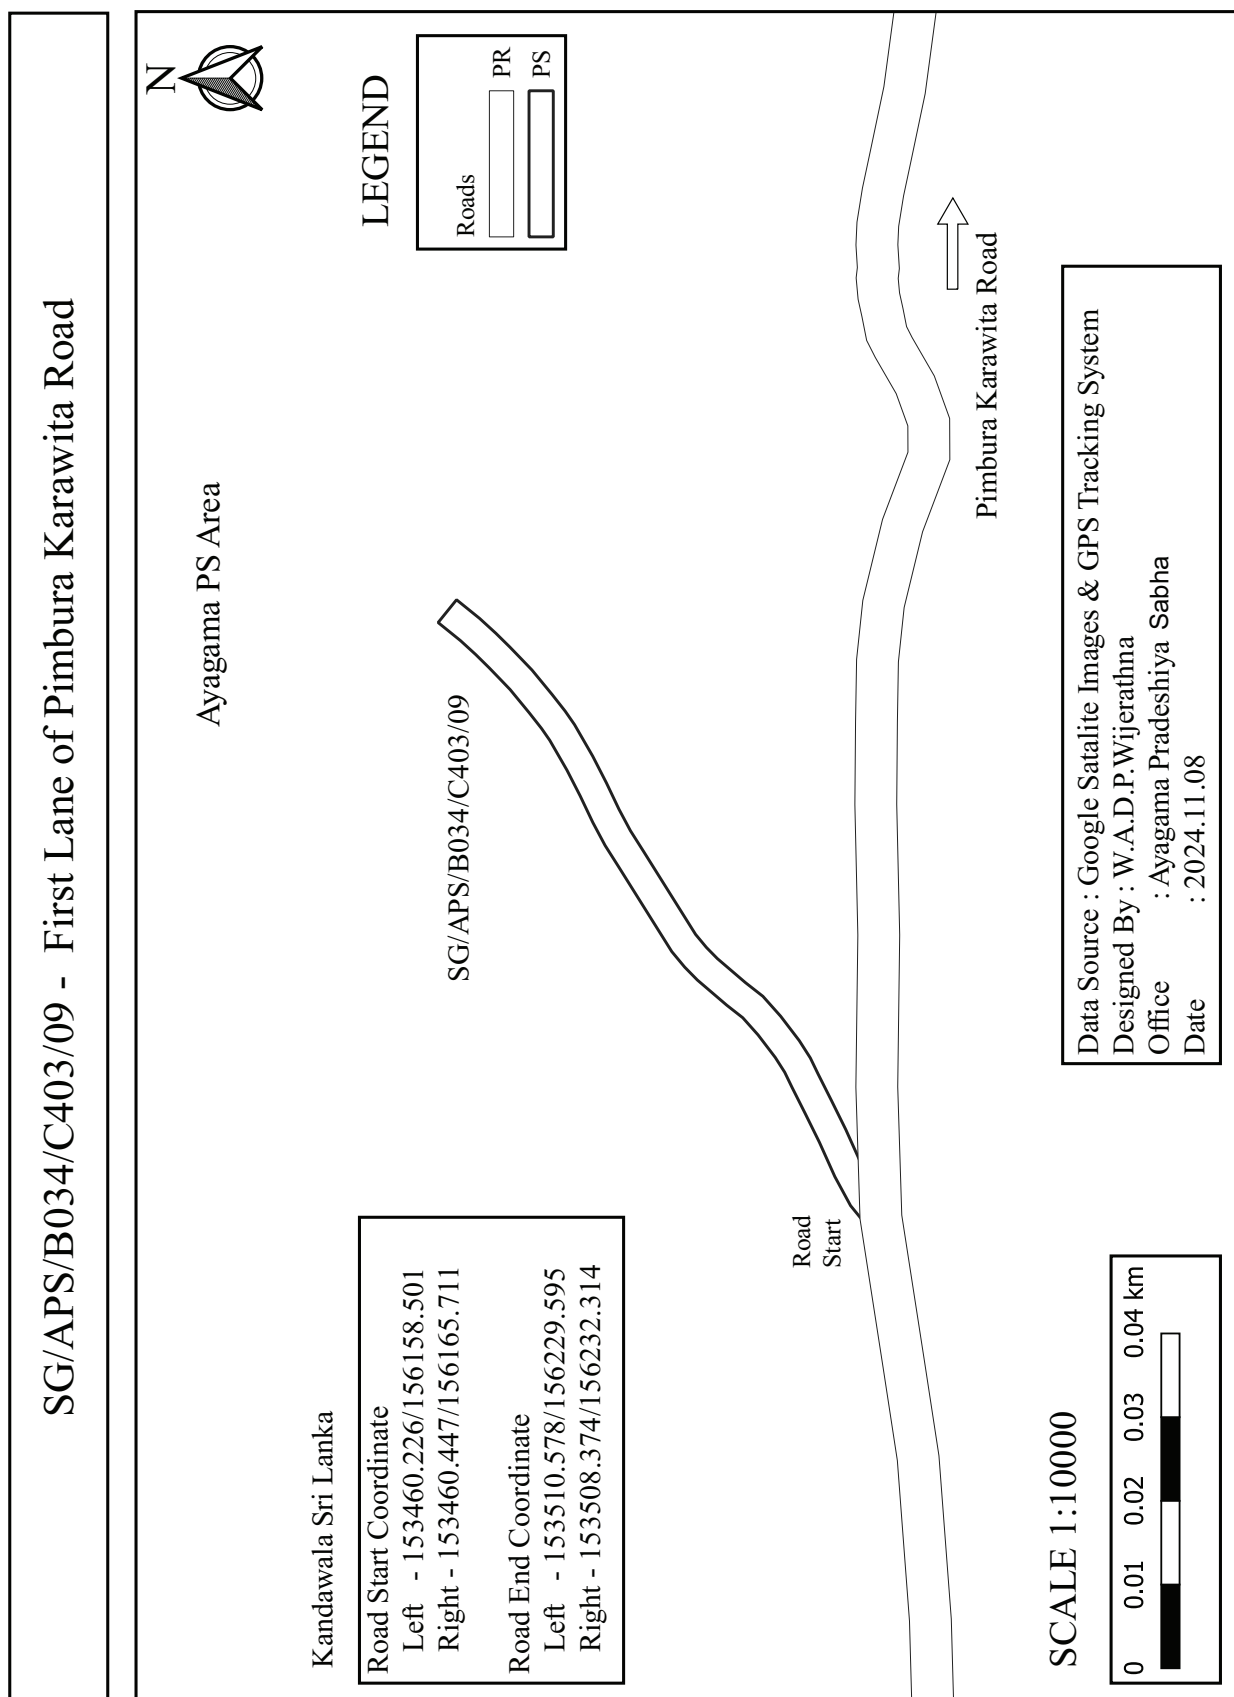



SG/APS/B421/C428/01 - First Lane of Kukulegama Jathuwangoda Road

