



ශ්‍රී ලංකා ප්‍රජාතාන්ත්‍රික සමාජවාදී ජනරජයේ ගැසට් පත්‍රය

இலங்கைச் சனநாயக சோசலிசக் குடியரசு வர்த்தமானப் பத்திரிகை

අති විශේෂ අති විශේෂමානතු

අංක 2469/29 - 2026 ජනවාරි 01 වැනි වසරේදී - 2025.01.01

2469/29 ஆம் இலக்கம் - 2026 ஆம் ஆண்டு சனவரி மாதம் 01 ஆந் திகதி வியாழக்கிழமை

(අරසාங்கத்தின் அதிகாரத்துடன் பிரசுரிக்கப்பட்டது)

பகுதி IV(ஆ) - உள்ளூராட்சி

உள்ளூராட்சி அறிவித்தல்கள்

அயகம பிரதேச சபை

1987 ஆம் ஆண்டின் 15 ஆம் இலக்க பிரதேச சபைகள் சட்டத்தின் 24 ஆம் பிரிவுடன் வாசிக்க வேண்டிய, சப்பிரகமுவ மாகாணத்தின் கௌரவ ஆளுநர் அவர்களால், 2023 ஆம் ஆண்டு சனவரி மாதம் 24 ஆம் திகதி 23/16 ஆம் இலக்கமுடைய அதி விசேட வர்த்தமானப் பத்திரிகையின் மூலம் பிரகடனப்படுத்தப்பட்டுள்ள “சப்பிரகமுவ மாகாணத்தின் பிரதேச சபைகளினால் பேணிச் செல்லப்படுகின்ற தெருக்கள் மற்றும் ஒடுக்கப் பாதைகளின் திட்டமிடல் விவகாரங்களை ஒழுங்கு செய்தல் மற்றும் பெயர்ப் பட்டியலைக் காட்சியளிக்கச் செய்து அறிவித்தல்களை பிரசுரித்தல் தொடர்பான கட்டளைகள்” தொகுப்பின் மூலம் சப்பிரகமுவ மாகாணத்தின் பிரதேச சபைகளுக்கு ஒப்படைக்கப்பட்டுள்ள பணிகளின்படி, இங்கு கீழ்க் காட்டப்பட்டுள்ள அட்டவணையில் உள்ளடங்கிய தெருக்கள் மற்றும் ஒடுக்கப் பாதைகள் அயகம பிரதேச சபைக்கு உரித்தாகியுள்ள தெருக்கள் மற்றும் ஒடுக்கப் பாதைகளாக பிரகடனப்படுத்த வேண்டுமென 2025.12.11 ஆம் திகதி நடத்தப்பட்ட சபைக்கூட்டத்தில் (06) 01.36 – II ஆம் இலக்கத்தின் கீழ் தீர்மானிக்கப்பட்டது என்பதை பொது மக்கள் அறிந்து கொள்வதற்காக இத்தால் விளம்பரப்படுத்தப்படுகின்றது.

மேற்கூறிய அட்டவணையில் உள்ளடங்கிய ஏதாவதொரு தெரு அல்லது ஒடுக்கப் பாதை ஏதாவதொரு காணியொன்றினூடாகச் செல்லும் அல்லது ஏதாவதொரு காணியின் ஒரு பகுதிக்கு உட்படுகிறது என்பதை தொடர்புடைய காணிக்கு உரிமை கூறுகின்றவர்களின் கருத்தாகுமாயின் மேற்கூறிய காணி தொடர்பில் தமக்குள்ள உரிமையை உறுதி செய்வதற்காக இவ்வறிவித்தற் திகதியிலிருந்து மூன்று மாத காலம் செல்வதற்கு முன் தகுந்த நீதிமன்றத்தில் வழக்கொன்றைத் தொடர்வதற்கான நடவடிக்கைகளை மேற்கொள்ள வேண்டும் என்பதையும் இத்தால் அறிவிக்கப்படுகின்றது.

மேலும் அதேபோன்று, மேற்கூறிய மூன்றுமாத கால எல்லை முடிவடைவதற்கு முன் அத்தகைய வழக்கொன்றை தொடராமல் இருக்கும் சந்தர்ப்பமொன்றில் மேற்கூறிய அட்டவணையில் உள்ளடங்கிய ஒவ்வொரு தெருவும், ஒடுக்கப் பாதையும் அயகம பிரதேச சபைக்குச் சொந்தமான தெருவொன்றாக அல்லது ஒடுக்கப் பாதையொன்றாகக் கருதப்படும் என்பதை மேலும் இத்தால் அறிவிக்கப்படுகின்றது.

ஏ.எம்.சி.கே. செனவிரத்தன,
செயலாளர்,
அயகம பிரதேச சபை.

பிரதேச சபை அலுவலகம்,
அயகம,
2025, திசம்பர் 30.

1A - PG7445 - 04 (2026/04)

இவ் அதிவிசேட வர்த்தமானியை www.documents.gov.lk எனும் இணையத்தளத்திலிருந்து பதிவிறக்கம் செய்ய முடியும்.

2A

IV (ஈ) கைபெ - ஸ்ரீ லக்ஷ்மீ பூசாநாதர் சமஸ்தானம் சிவரத்தினம் - 2026.01.01

பகுதி IV (ஆ) - இலங்கைச் சனநாயக சோசலிசக் குடியரசு வர்த்தமானப் பத்திரிகை - அதி விசேஷமானது - 2026.01.01

தொ. இல.	தெருவின் குறியீடு	தெருவின் பெயர்	ஆரம்ப தொகுதி இலக்கங்கள் (கந்தவல இலங்கை)		இறுதித் தொகுதி இலக்கங்கள் (கந்தவல இலங்கை)		பாதை பொது வான அகலம் (மீற்றர்)	பாதை பொது வான அகலம் (மீற்றர்)	அபி விருத்தி அகலம் (மீற்றர்)
			இடம்	வலம்	இடம்	வலம்			
1	SG/APS/ B034/ 01	பெல்லிமோதரவத்த தெரு	159876.947/ 148983.413	159874.112/ 148984.555	159905.907/ 149885.744	159906.975/ 149882.939	3.0	3.0	2.5
2	SG/APS/ B034/ 01/ 01	பெல்லிமோதரவத்த கிராம சபைத் தெரு	159877.497/ 149042.944	159878.751/ 149049.381	160030.782/ 149513.286	160027.886/ 149512.507	3.0	3.0	2.5
3	SG/APS/ B034/ 02	அயகம் 08 ஏக்கர் யக்கஹட்டுவெல தெரு	159776.853/ 149052.16	159779.998/ 149049.682	160468.738/ 147891.991	160465.818/ 147894.809	4.0	4.0	3.0
4	SG/APS/ B034/ 02/ 01	மஹபேருவ கந்த தெரு	159735.011/ 149000.084	159735.439/ 148996.823	159373.122/ 148527.286	159375.522/ 148525.486	3.0	3.0	2.0
5	SG/APS/ B034/ 02/ 02	வெரணியகெட்டிய தெரு	159881.887/ 148705.505	159880.342/ 148701.478	159569.287/ 148483.953	159571.939/ 148486.947	4.0	4.0	2.5
6	SG/APS/ B034/ 02/ 02/ 01	வெரணியகெட்டிய தெருவின் முதலாம் ஒழுங்கை	159700.651/ 148621.953	159697.668/ 148622.287	159689.727/ 148674.064	159686.763/ 148674.528	3.0	3.0	2.8
7	SG/APS/ B034/ 02/ 02/ 02	வெரணியகெட்டிய தெருவின் இரண்டாம் ஒழுங்கை	159676.864/ 148629.875	159670.766/ 148631.369	159648.827/ 148658.334	159645.965/ 148659.235	3.0	3.0	3.0
8	SG/APS/ B034/ 02/ 03	08 ஏக்கர் தெரு	159896.163/ 148288.035	159893.565/ 148284.896	159044.8/ 148734.409	159043.773/ 148730.109	4.0	4.0	3.5

தொ. இல.	தெருவின் குறியீடு	தெருவின் பெயர்	ஆரம்ப தொகுதி இலக்கங்கள் (கந்தவல இலங்கை)		இறுதித் தொகுதி இலக்கங்கள் (கந்தவல இலங்கை)		பாறை பொது வான நிலம் (மீற்றர்)	பாறை பொது வான அகலம் (மீற்றர்)	அபி விருத்தி அகலம் (மீற்றர்)
			இடம்	வலம்	இடம்	வலம்			
9	SG/ APS/ B034/ 02/ 04	வத்தஇன்னகந்த கீழ் தெரு	159879.35/ 148221.045	159877.375/ 148218.784	159479.305/ 148252.167	159476.739/ 148250.614	422.79	3.0	2.7
10	SG/ APS/ B034/ 02/ 05	08 ஏக்கர் வத்தஇன்னகந்த தெரு	159863.257/ 148197.441	159863.872/ 148193.483	159857.93/ 147900.482	159859.376/ 147904.212	435.75	4.0	3.0
11	SG/ APS/ B034/ 02/ 05/ 01	08 ஏக்கர் வத்தஇன்னகந்த தெருவின் முதலாம் ஒழுங்கை	159717.39/ 148002.043	159718.897/ 147999.446	159572.467/ 147803.659	159574.459/ 147799.764	258.78	3.0	2.0
12	SG/ APS/ B034/ 02/ 06	கித்துலகல ஓகந்த தெரு	159927.749/ 148107.283	159930.172/ 148103.793	159871.823/ 148055.912	159875.25/ 148053.849	79.09	4.0	3.0
13	SG/ APS/ B034/ 02/ 06/ 01	கித்துலகல ஓகந்த தெருவின் முதலாம் ஒழுங்கை	159872.751/ 148055.319	159874.309/ 148054.416	159846.304/ 148065.139	159845.591/ 148063.488	48.08	1.8	1.8
14	SG/ APS/ B034/ 02/ 07	வத்தஇன்னகந்த தெரு	160406.523/ 147812.894	160410.882/ 147813.516	159301.816/ 147931.145	159305.283/ 147929.148	1514.7	4.0	3.5
15	SG/ APS/ B034/ 02/ 07/ 01	கெக்குணாகஹ ஹேன தெரு	160409.473/ 147806.227	160410.098/ 147810.406	160319.044/ 147126.992	160322.993/ 147126.359	1036.92	4.0	3.5
16	SG/ APS/ B034/ 02/ 07/ 02	சுனிமலாராம தெரு	160275.603/ 147707.697	160279.735/ 147709.571	160452.02/ 147575.579	160454.159/ 147578.349	228.15	3.5	2.6

4A

IV (ஈ) கைபெ - ஸ்ரீ லக்ஷ்மீ பூசாநாதர் சமஸ்தானம் ஸ்ரீ லக்ஷ்மீ பூசாநாதர் சமஸ்தானம் - 2026.01.01

பகுதி IV (ஆ) - இலங்கைச் சனநாயக சோசலிசக் குடியரசு வர்த்தமானப் பத்திரிகை - அதி விசேஷமானது - 2026.01.01

தொ. இல.	தெருவின் குறியீடு	தெருவின் பெயர்	ஆரம்ப தொகுதி இலக்கங்கள் (கந்தவல இலங்கை)		இறுதித் தொகுதி இலக்கங்கள் (கந்தவல இலங்கை)		பாதை பொது வான அகலம் (மீற்றர்)	அபி விருத்தி அகலம் (மீற்றர்)
			இடம்	வலம்	இடம்	வலம்		
17	SG/APS/ B034/ 02/ 07/ 03	வத்தின்குளம் தெருவின் முதலாம் ஒழுங்கை	160123.442/ 147596.918	160124.761/ 147599.693	160270.834/ 147498.315	160271.575/ 147501.222	3.0	3.0
18	SG/APS/ B034/ 02/ 07/ 04	மல்வெல கிளைவழி ஒற்றையடிப் பாதை	160115.296/ 147583.669	160117.421/ 147586.06	160080.563/ 147501.059	160083.058/ 147499.39	3.0	2.0
19	SG/APS/ B034/ 02/ 07/ 05	வத்தின்குளம் தெருவின் கெக்குண்குளம் தெரு	160029.201/ 147534.248	160032.641/ 147535.317	160417.467/ 147281.162	160415.341/ 147284.577	3.5	3.0
20	SG/APS/ B034/ 03	கால்நடை வைத்திய உத்தியோகத்தர் அலுவலகத் தெரு	159683.217/ 149143.266	159678.225/ 149151.754	159574.286/ 149243.05	159578.091/ 149243.562	4.0	3.0
21	SG/APS/ B034/ 04	நிறைந்தமானிகம் சமருகம் தொண்டுகோட்ட தெரு	159499.955/ 149200.61	159496.052/ 149199.269	159377.076/ 149566.606	159379.326/ 149570.003	4.0	3.5
22	SG/APS/ B034/ 04/ 01	சரத்புரம் முதலாம் ஒழுங்கை	159471.165/ 149219.603	159466.88/ 149220.591	159469.014/ 149295.972	159465.021/ 149295.734	4.0	3.0
23	SG/APS/ B034/ 04/ 02	சரத்புரம் இரண்டாம் ஒழுங்கை	159392.077/ 149223.459	159390.157/ 149224.139	159356.266/ 149288.908	159352.841/ 149289.672	2.0	1.0
24	SG/APS/ B034/ 04/ 03	கொரட்டு வத்த தெரு	159250.253/ 149314.197	159256.987/ 149315.207	159249.113/ 149289.054	159251.528/ 149289.703	2.5	2.0

தொ. இல.	தெருவின் குறியீடு	தெருவின் பெயர்	ஆரம்ப தொகுதி இலக்கங்கள் (கந்தவல இலங்கை)		இறுதித் தொகுதி இலக்கங்கள் (கந்தவல இலங்கை)		பாறை பொது வான நிலம் (மீற்றர்)	பாறை பொது வான நிலம் (மீற்றர்)	அபி விருத்தி அகலம் (மீற்றர்)
			இடம்	வலம்	இடம்	வலம்			
25	SG/ APS/ B034/ 04/ 04	சாத்தூரில் இருந்து மயானம் வரையுள்ள பாறை	159117.957/ 149522.031	159116.825/ 149524.857	159275.288/ 149566.638	159273.2/ 149568.792	187.03	3.0	3.0
26	SG/ APS/ B034/ 04/ 05	நிறைத்தமானிகம் கீழ் வளைவுப் பாறை	159058.681/ 149552.921	159061.605/ 149551.934	159020.189/ 149590.958	159018.534/ 149593.463	460.36	3.0	3.0
27	SG/ APS/ B034/ 04/ 06	நிறைத்தமானிகம் பெரலியன தெரு	158983.715/ 149677.2	158982.347/ 149673.256	158383.276/ 149913.921	158381.918/ 149910.023	833.08	4.0	3.5
28	SG/ APS/ B034/ 04/ 06/ 01	மஹேன தோட்டத் தெரு	158964.351/ 149692.745	158961.299/ 149694.296	158998.977/ 150099.954	158996.351/ 150101.403	544.1	3.0	3.0
29	SG/ APS/ B034/ 04/ 07	சமருகம் மயானப் பாறை	159222.068/ 149663.818	159222.56/ 149662.789	159167.768/ 149577.524	159169.575/ 149577.603	109.07	1.0	1.0
30	SG/ APS/ B034/ 05	17 ஏக்கர் தெரு	159211.519/ 149034.985	159218.216/ 149030.927	159041.303/ 148733.53	159047.967/ 148731.88	414.34	4.0	3.0
31	SG/ APS/ B034/ 05/ 01	17 ஏக்கர் தெருவின் முதலாம் ஒழுங்கை	159130.998/ 148885.536	159127.121/ 148884.22	159083.254/ 148926.653	159080.254/ 148924.85	66.63	3.5	3.0
32	SG/ APS/ B034/ 05/ 02	17 ஏக்கர் தெருவின் உடுவக்கந்த தெரு	159044.8/ 148734.409	159043.773/ 148730.109	158125.354/ 149478.274	158121.421/ 149477.302	1973.6	4.0	3.0

6A

IV (ஈ) கைபெ - ஸ்ரீ லக்ஷ்மீ ப்ரதாபநிதி சபாபலாடி ப்ரதாபநிதி - 2026.01.01

பகுதி IV (ஆ) - இலங்கைச் சனநாயக சோசலிசக் குடியரசு வர்த்தமானப் பத்திரிகை - அதி விசேஷமானது - 2026.01.01

தொ. இல.	தெருவின் குறியீடு	தெருவின் பெயர்	ஆரம்ப தொகுதி இலக்கங்கள் (கந்தவல இலங்கை)		இறுதித் தொகுதி இலக்கங்கள் (கந்தவல இலங்கை)		பாதை பொது வான அகலம் (மீற்றர்)	அபி விருத்தி அகலம் (மீற்றர்)
			இடம்	வலம்	இடம்	வலம்		
33	SG/APS/ B034/ 05/ 02/ 01	17 ஏக்கர் உடுவக்கந்த தெருவின் முதலாம் ஒழுங்கை	159021.748/ 148734.947	159025.062/ 148734.705	158796.759/ 148656.29	158795.047/ 148653.825	3.0	2.0
34	SG/APS/ B034/ 05/ 02/ 01/ 01	17 ஏக்கர் உடுவக்கந்த தெருவின் முதலாம் ஒழுங்கையின் முதலாம் கிளைவழி	158991.422/ 148548.772	158992.385/ 148549.052	159057.796/ 148519.906	159058.97/ 148519.778	1.0	1.0
35	SG/APS/ B034/ 05/ 02/ 02	17 ஏக்கர் பலிகல தலபுத்தல தெரு	158790.021/ 148650.333	158794.837/ 148653.525	158382.198/ 147780.059	158385.922/ 147778.599	4.0	3.0
36	SG/APS/ B034/ 05/ 02/ 02/ 01	17 ஏக்கர் பலிகல தலபுத்தல தெருவின் முதலாம் ஒழுங்கை	158817.423/ 148519.898	158817.439/ 148528.493	158838.804/ 148127.09	158822.184/ 148132.745	4.0	3.0
37	SG/APS/ B034/ 05/ 02/ 03	17 ஏக்கர் உடுவக்கந்த தெருவின் இரண்டாம் ஒழுங்கை	158438.414/ 148763.884	158435.909/ 148765.709	158503.197/ 148862.357	158500.647/ 148860.779	3.0	3.0
38	SG/APS/ B034/ 06	எரேபோருவ முதல் தெரு	158948.58/ 149198.35	158950.482/ 149197.656	158925.977/ 149044.689	158927.188/ 149046.282	2.0	2.0
39	SG/APS/ B034/ 07	ஹங்கமுல்ல எரேபோருவ தெரு	158756.919/ 149280.358	158751.859/ 149280.624	158853.235/ 149666.474	158851.455/ 149670.328	4.0	3.0
40	SG/APS/ B034/ 08	பத்தலவத்த தெரு	158734.228/ 149276.134	158737.683/ 149275.567	159079.02/ 148828.925	159080.342/ 148832.184	3.5	3.0

தொ. இல.	தெருவின் குறியீடு	தெருவின் பெயர்	ஆரம்ப தொகுதி இலக்கங்கள் (கந்தவல இலங்கை)		இறுதித் தொகுதி இலக்கங்கள் (கந்தவல இலங்கை)		பாறை பொது வான நிலம் (மீற்றர்)	பாறை பொது வான அகலம் (மீற்றர்)	அபி விருத்தி அகலம் (மீற்றர்)
			இடம்	வலம்	இடம்	வலம்			
41	SG/ APS/ B034/ 09	பெரலியன நெகிரிகந்த தெரு	158343.692/ 149536.821	158333.851/ 149536.613	157532.409/ 151660.94	157528.419/ 151661.227	3194.99	4.0	3.0
42	SG/ APS/ B034/ 09/ 01	பெரலியன நெகிரிகந்த தெருவின் முதலாம் ஒழுங்கை	158588.658/ 150216.398	158590.104/ 150219.052	158692.325/ 150185.096	158693.417/ 150187.89	110.23	3.0	2.0
43	SG/ APS/ B034/ 09/ 02	பெரலியன நெகிரிகந்த தெருவின் இரண்டாம் ஒழுங்கை	158627.329/ 150277.199	158626.656/ 150280.344	158689.683/ 150433.452	158692.408/ 150432.198	351.56	3.0	3.0
44	SG/ APS/ B034/ 09/ 03	பெரலியன நெகிரிகந்த தெருவின் மூன்றாம் ஒழுங்கை	158111.976/ 150987.353	158112.465/ 150991.438	158275.157/ 151205.948	158271.209/ 151206.585	306.03	4.0	3.0
45	SG/ APS/ B034/ 09/ 03/ 01	பெரலியன நெகிரிகந்த தெருவின் மூன்றாம் ஒழுங்கையின் முதல் கிளைத்தெரு	158154.744/ 150992.508	158156.61/ 150997.015	158299.236/ 150956.415	158301.233/ 150959.881	161.88	4.0	3.0
46	SG/ APS/ B034/ 09/ 04	பெரலியன நெகிரிகந்த தெருவின் நான்காம் ஒழுங்கை	157834.276/ 151232.737	157836.717/ 151228.902	157712.493/ 151213.456	157714.3/ 151209.888	141.11	4.0	4.0
47	SG/ APS/ B034/ 09/ 05	பெரலியன நெகிரிகந்த தெருவின் ஐந்தாம் ஒழுங்கை	157738.073/ 151409.432	157739.279/ 151405.489	157651.773/ 151359.443	157651.821/ 151355.433	103.89	4.0	4.0
48	SG/ APS/ B034/ 09/ 06	பெரலியன நெகிரிகந்த தெருவின் ஆறாம் ஒழுங்கை	157740.857/ 151414.172	157738.739/ 151412.038	157645.585/ 151601.7	157643.157/ 151603.606	236.88	3.0	3.0

8A

IV (ஈ) கைபெ - ஸ்ரீ லக்ஷ்மீ பூசாநாதர் சமஸ்தான ஸ்தலபீத பரபீத - 2026.01.01

பகுதி IV (ஆ) - இலங்கைச் சனநாயக சோசலிசக் குடியரசு வர்த்தமானப் பத்திரிகை - அதி விசேஷமானது - 2026.01.01

தொ. இல.	தெருவின் குறியீடு	தெருவின் பெயர்	ஆரம்ப தொகுதி இலக்கங்கள் (கந்தவல இலங்கை)		இறுதித் தொகுதி இலக்கங்கள் (கந்தவல இலங்கை)		பாறை பொது வான அகலம் (மீற்றர்)	பாறை பொது வான அகலம் (மீற்றர்)	அபி விருத்தி அகலம் (மீற்றர்)
			இடம்	வலம்	இடம்	வலம்			
49	SG/APS/ B034/ 10	மதனகொடை தொடக்கம் உடுகல வரையிலான தெரு	158181.837/ 149530.177	158184.494/ 149528.738	157391.423/ 149936.971	157396.102/ 149933.757	3.0	3.0	3.0
50	SG/APS/ B034/ 10/ 01	மதனகொடை தொடக்கம் உடுகல வரையிலான தெருவின் முதலாம் ஒழுங்கை	158011.146/ 149532.548	158013.627/ 149532.226	158005.128/ 149421.695	158007.541/ 149422.344	2.5	2.5	2.5
51	SG/APS/ B034/ 10/ 02	பரகல ஒவிட்ட முதல் ஒழுங்கைத் தெரு	157873.215/ 149556.686	157875.354/ 149554.572	157702.551/ 149441.812	157700.574/ 149439.557	3.0	3.0	3.0
52	SG/APS/ B034/ 10/ 02/ 01	பரகல ஒவிட்ட முதல் ஒழுங்கையின் கிளைத்தெரு	157863.022/ 149546.611	157866.47/ 149548.22	157875.338/ 149462.628	157875.905/ 149465.575	3.0	3.0	3.0
53	SG/APS/ B034/ 10/ 03	பரகல ஒவிட்ட இரண்டாம் ஒழுங்கை	157834.076/ 149624.615	157835.474/ 149621.555	157643.499/ 149637.885	157644.625/ 149635.105	3.0	3.0	3.0
54	SG/APS/ B034/ 10/ 04	மதனகொட தொடக்கம் உடுகல வரையிலான தெருவின் இரண்டாம் ஒழுங்கை	157572.746/ 149848.72	157574.867/ 149848.169	157407.661/ 149823.444	157411.3/ 149823.103	2.0	2.0	2.0
55	SG/APS/ B034/ 11	சிறிவர்தன தோட்டம் முதலாம் ஒழுங்கை	158119.974/ 149611.359	158117.772/ 149613.678	158097.966/ 150266.167	158097.965/ 150269.167	3.0	3.0	3.0
56	SG/APS/ B034/ 11/ 01	சிறிவர்தன தோட்டம் முதலாம் தெருவின் முதல் ஒழுங்கை	158165.277/ 149982.886	158164.765/ 149979.875	158001.442/ 150157.23	158000.977/ 150154.266	3.0	3.0	3.0

தொ. இல.	தெருவின் குறியீடு	தெருவின் பெயர்	ஆரம்ப தொகுதி இலக்கங்கள் (கந்தவல இலங்கை)		இறுதித் தொகுதி இலக்கங்கள் (கந்தவல இலங்கை)		பாறை பொது வான நிலம் (மீற்றர்)	பாறை பொது வான நிலம் (மீற்றர்)	அபி விருத்தி அகலம் (மீற்றர்)
			இடம்	வலம்	இடம்	வலம்			
57	SG/ APS/ B034/ 11/ 02	சிறிவர்தன தோட்டம் முதலாம் தெருவின் இரண்டாம் ஒழுங்கை	158183.877/ 150138.891	158183.701/ 150135.855	158056.203/ 150194.002	158054.299/ 150191.685	155.02	3.0	2.0
58	SG/ APS/ B034/ 12	சிறிவர்தன தோட்டம் இரண்டாம் தெரு	158067.32/ 149668.969	158064.904/ 149672.168	158155.149/ 149764.095	158152.044/ 149766.619	132.98	4.0	3.7
59	SG/ APS/ B034/ 13	சிறிவர்தன தோட்டம் மூன்றாம் தெரு	157819.709/ 149904.392	157818.331/ 149909.932	157908.052/ 149997.177	157909.043/ 150000.008	188.4	3.0	3.0
60	SG/ APS/ B034/ 14	கெக்குலம் தெரு	157692.678/ 150117.011	157690.766/ 150120.01	157859.924/ 150207.02	157859.935/ 150210.02	209.84	3.0	2.5
61	SG/ APS/ B034/ 15	உடுகல 700 ஆம் தோட்டத் தெரு	157472.011/ 150400.013	157465.682/ 150409.027	158082.002/ 150937.345	158082.049/ 150940.482	1152.86	3.0	2.6
62	SG/ APS/ B034/ 16	உடுகல மயானப் பாறை	157213.578/ 150638.917	157209.917/ 150640.688	157473.954/ 150759.872	157471.31/ 150762.871	441.99	4.0	3.0
63	SG/ APS/ B034/ 16/ 01	உடுகல மயானப் பாறையின் முதல் ஒழுங்கை	157441.317/ 150680.703	157443.508/ 150682.996	157490.669/ 150671.598	157491.717/ 150674.145	55.95	2.8	2.8
64	SG/ APS/ B034/ 17	உடுகல புதிய குடியேற்றத் தெரு	157184.913/ 150645.936	157180.588/ 150644.712	157214.234/ 151039.016	157211.488/ 151036.106	537.82	4.0	3.0

தொ. இல.	தெருவின் குறியீடு	தெருவின் பெயர்	ஆரம்ப தொகுதி இலக்கங்கள் (கந்தவல இலங்கை)		இறுதித் தொகுதி இலக்கங்கள் (கந்தவல இலங்கை)		பாதை பொது வான நீளம் (மீற்றர்)	பாதை பொது வான அகலம் (மீற்றர்)	அபி விருத்தி அகலம் (மீற்றர்)
			இடம்	வலம்	இடம்	வலம்			
65	SG/APS/ B034/ 17/ 01	உடுகல் புதிய குடியேற்றத் தெருவின் முதல் ஒழுங்கை	157136.225/ 150717.328	157134.024/ 150715.029	157115.616/ 150802.37	157112.682/ 150802.997	126.93	3.0	3.0
66	SG/APS/ B034/ 17/ 02	உடுகல் புதிய குடியேற்றத் தெருவின் இரண்டாம் ஒழுங்கை	157194.701/ 150840.201	157193.513/ 150842.97	157258.397/ 150834.561	157258.816/ 150837.531	67.31	3.0	3.0
67	SG/APS/ B034/ 17/ 03	உடுகல் புதிய குடியேற்றத் தெருவின் மூன்றாம் ஒழுங்கை	157179.764/ 150851.724	157183.032/ 150849.121	157144.654/ 150802.344	157146.314/ 150798.704	64.78	4.0	3.0
68	SG/APS/ B034/ 17/ 04	உடுகல் புதிய குடியேற்றத் தெருவின் நான்காம் ஒழுங்கை	157200.963/ 150891.536	157203.824/ 150894.019	157287.029/ 150857.015	157287.488/ 150859.98	97.11	3.0	3.0
69	SG/APS/ B034/ 17/ 05	உடுகல் புதிய குடியேற்றத் தெருவின் ஐந்தாம் ஒழுங்கை	157216.086/ 150916.647	157213.762/ 150913.39	157127.214/ 150981.919	157125.388/ 150978.36	123.59	4.0	3.0
70	SG/APS/ B034/ 18	20 ஏக்கர் தெரு	156877.268/ 150804.353	156877.963/ 150800.9	156656.696/ 150684.219	156654.526/ 150679.967	304.82	3.5	3.0
71	SG/APS/ B034/ 19	பரகல தேயிலைத் தொழிற்சாலைத் தெரு	156572.965/ 151531.534	156566.092/ 151530.921	156786.029/ 151735.844	156782.224/ 151737.077	510.48	4.0	3.5
72	SG/APS/ B034/ 20	மாணகந்த தவலகெட்டிய பரகல தோட்டத் தெரு	156360.177/ 151676.944	156359.953/ 151672.728	155883.786/ 151411.51	155887.773/ 151411.84	611.81	4.0	2.6

தொ. இல.	தெருவின் குறியீடு	தெருவின் பெயர்	ஆரம்ப தொகுதி இலக்கங்கள் (கந்தவல இலங்கை)		இறுதித் தொகுதி இலக்கங்கள் (கந்தவல இலங்கை)		பாறை பொது வான நிலம் (மீற்றர்)	பாறை பொது வான நிலம் (மீற்றர்)	அபி விருத்தி அகலம் (மீற்றர்)
			இடம்	வலம்	இடம்	வலம்			
73	SG/ APS/ B034/ 20/ 01	பரகல கோடிகெதர தோட்டத் தெரு	156168.376/ 151640.022	156171.544/ 151642.503	156236.059/ 151404.622	156238.258/ 151401.282	358.16	4.0	2.5
74	SG/ APS/ B034/ 20/ 02	பரகல மானகந்த தெரு	156169.797/ 151646.132	156166.453/ 151643.627	155789.695/ 151426.375	155792.419/ 151429.304	593.3	4.0	2.5
75	SG/ APS/ B034/ 20/ 02/ 01	பரகல கெசெல்கொட்டுவ தெரு	156157.289/ 151679.199	156154.634/ 151682.46	156034.065/ 151783.759	156034.102/ 151780.759	207.91	3.0	2.0
76	SG/ APS/ B034/ 20/ 02/ 02	பரகல மானகந்த தெருவின் முதல் ஒழுங்கை	156010.801/ 151671.013	156007.863/ 151670.303	155883.58/ 151868.857	155881.899/ 151871.343	342.96	3.0	2.4
77	SG/ APS/ B034/ 20/ 02/ 03	பரகலகந்த தெரு	155843.954/ 151581.64	155840.732/ 151579.269	155314.994/ 151842.066	155311.916/ 151839.512	638.21	4.0	2.5
78	SG/ APS/ B034/ 20/ 02/ 04	மானகந்த பரகலகந்த தெரு	155772.657/ 151521.694	155771.718/ 151517.214	155589.382/ 151354.958	155591.602/ 151352.94	284.75	3.0	1.0
79	SG/ APS/ B034/ 21	பரகல கலஉடகந்த நிரிஸல்ல தெரு	156373.909/ 151711.103	156373.201/ 151716.646	156792.033/ 153926.13	156788.576/ 153926.675	2579.91	3.5	3.0
80	SG/ APS/ B034/ 21/ 01	கொடிகார பங்குவ தெரு	156538.424/ 151964.35	156536.76/ 151960.071	156381.863/ 151983.084	156385.862/ 151982.999	214.84	4.0	2.5

12A

IV (ஈ) கைபெ - ஸ்ரீ லக்ஷ்மீ ப்ரதீபாதிபதி கலாச்சலாதிபதி ப்ரதீபாதிபதி - 2026.01.01

பகுதி IV (ஆ) - இலங்கைச் சனநாயக சோசலிசக் குடியரசு வர்த்தமானப் பத்திரிகை - அதி விசேஷமானது - 2026.01.01

தொ. இல.	தெருவின் குறியீடு	தெருவின் பெயர்	ஆரம்ப தொகுதி இலக்கங்கள் (கந்தவல இலங்கை)		இறுதித் தொகுதி இலக்கங்கள் (கந்தவல இலங்கை)		பாறை பொது வான அகலம் (மீற்றர்)	பாறை பொது வான அகலம் (மீற்றர்)	அபி விருத்தி அகலம் (மீற்றர்)
			இடம்	வலம்	இடம்	வலம்			
81	SG/APS/ B034/ 21/ 02	கிவ்லேனை கொடிகார பங்குவ தெரு	156546.391/ 152043.263	156548.149/ 152048.114	156787.385/ 151893.95	156791.09/ 151895.46	310.94	4.0	3.0
82	SG/APS/ B034/ 21/ 02/ 01	கிவ்லேனை கொடிகார பங்குவ தெருவின் முதல் ஒழுங்கை	156598.289/ 152032.348	156594.757/ 152034.194	156898.787/ 152008.165	156898.007/ 152011.062	321.58	3.0	2.0
83	SG/APS/ B034/ 21/ 03	கலஉட கந்த முதல் ஒழுங்கை	156571.617/ 152309.337	156570.741/ 152312.83	156623.027/ 152278.37	156626.563/ 152277.695	83.32	3.6	3.0
84	SG/APS/ B034/ 21/ 04	கலஉட கந்த பத்தலவத்த தெரு	156573.555/ 152773.207	156574.564/ 152768.959	156404.175/ 152802.831	156402.073/ 152799.428	188.43	4.0	3.5
85	SG/APS/ B034/ 21/ 05	பரகல கலஉடகந்த நிரிளில் அரம்ப ஒற்றையடிப் பாறை	156607.192/ 152840.292	156608.18/ 152843.295	156645.905/ 152795.527	156648.802/ 152796.306	65.93	3.0	2.5
86	SG/APS/ B034/ 22	பரகல அமுலேனை கந்த தெரு	156311.263/ 151852.193	156308.847/ 151853.986	156339.724/ 151947.712	156337.826/ 151949.633	114.43	2.7	2.5
87	SG/APS/ B034/ 23	பரகல அமுலேனை தெரு	156018.482/ 152154.787	156015.62/ 152153.686	156165.389/ 152193.153	156167.56/ 152195.224	280.02	3.0	2.5
88	SG/APS/ B034/ 24	பரகல பொக்குணுதொல தெரு	155906.959/ 152234.496	155903.953/ 152235.52	156005.52/ 152398.007	156004.741/ 152400.905	221.13	3.0	2.5

தொ. இல.	தெருவின் குறியீடு	தெருவின் பெயர்	ஆரம்ப தொகுதி இலக்கங்கள் (கந்தவல இலங்கை)		இறுதித் தொகுதி இலக்கங்கள் (கந்தவல இலங்கை)		பாறை பொது வான நிலம் (மீற்றர்)	பாறை பொது வான அகலம் (மீற்றர்)	அபி விருத்தி அகலம் (மீற்றர்)
			இடம்	வலம்	இடம்	வலம்			
89	SG/ APS/ B034/ 25	பரகல கிரிமெட்டி ஹேன தெரு	155605.488/ 152254.823	155610.423/ 152254.601	155213.861/ 151898.401	155212.207/ 151895.898	756	3.0	2.6
90	SG/ APS/ B034/ 26	மீனமல்வத்த கலஉடகந்த தெரு	155548.83/ 152342.896	155544.417/ 152344.581	156481.018/ 152489.773	156485.08/ 152492.253	1680	4.0	3.0
91	SG/ APS/ B034/ 26/ 01	கெவத்தேஹன தெரு முதல் ஒழுங்கை	155812.259/ 152854.083	155807.217/ 152852.988	155881.989/ 152886.323	155882.927/ 152890.212	90.69	4.0	3.0
92	SG/ APS/ B034/ 26/ 02	கெவத்தேஹன தெரு இரண்டாம் ஒழுங்கை	156137.361/ 152707.502	156135.173/ 152709.799	156172.151/ 152815.675	156169.384/ 152814.517	151.73	3.0	3.0
93	SG/ APS/ B034/ 26/ 03	கெவத்தேஹன தெரு மூன்றாம் ஒழுங்கை	156141.391/ 152699.11	156145.003/ 152698.151	156061.22/ 152612.179	156064.117/ 152612.958	148.28	3.0	2.5
94	SG/ APS/ B034/ 27	குருகடேஹன தெரு	155206.007/ 152563.527	155204.082/ 152567.05	155242.19/ 152686.466	155238.344/ 152687.568	154.24	4.0	3.5
95	SG/ APS/ B034/ 28	பீல்வத்த முதல் ஒழுங்கை	154869.536/ 152691.801	154873.824/ 152690.24	154751.073/ 152596.152	154754.425/ 152598.333	221.14	4.0	3.5
96	SG/ APS/ B034/ 29	ஐந்தாம் மைல் கம்பம் மேல் தெரு	154809.16/ 152802.307	154805.185/ 152807.601	154907.573/ 152813.606	154908.043/ 152817.578	124.81	4.0	2.0

தொ. இல.	தெருவின் குறியீடு	தெருவின் பெயர்	ஆரம்ப தொகுதி இலக்கங்கள் (கந்தவல இலங்கை)		இறுதித் தொகுதி இலக்கங்கள் (கந்தவல இலங்கை)		பாதை பொது வான அகலம் (மீற்றர்)	அபி விருத்தி அகலம் (மீற்றர்)
			இடம்	வலம்	இடம்	வலம்		
97	SG/APS/ B034/ 30	புஸ்ஸல கந்த தெரு	154427.166/ 153082.404	154420.883/ 153083.167	155488.137/ 152921.174	155487.906/ 152925.667	4.5	4.0
98	SG/APS/ B034/ 30/ 01	புஸ்ஸல கந்த அன்னாசிகல தெரு	154792.381/ 153158.865	154787.287/ 153159.596	154753.1/ 153504.337	154749.634/ 153506.333	4.0	3.5
99	SG/APS/ B034/ 30/ 01/ 01	புஸ்ஸல கந்த அன்னாசிகல தெருவின் முதல் ஒழுங்கை	154742.638/ 153222.09	154745.056/ 153218.001	154408.76/ 153347.892	154408.756/ 153343.891	4.0	3.5
100	SG/APS/ B034/ 30/ 02	புஸ்ஸல கந்த சனசமூக நிலையத் தெரு	154998.718/ 153197	154993.134/ 153197.319	155037.456/ 153256.341	155035.567/ 153259.866	4.0	3.5
101	SG/APS/ B034/ 30/ 03	புஸ்ஸல கந்த முதல் ஒழுங்கை	155179.961/ 153156.997	155176.157/ 153158.242	155353.978/ 153314.694	155349.98/ 153314.623	4.0	3.5
102	SG/APS/ B034/ 31	பீல்ல வத்த தெரு	154406.068/ 153077.414	154411.176/ 153077.68	154202.873/ 152646.25	154203.992/ 152642.41	4.0	3.0
103	SG/APS/ B034/ 31/ 01	மணல் அகழும் ஆற்றுத்துறை	154338.58/ 152979.364	154338.638/ 152974.272	154245.307/ 153028.339	154245.823/ 153024.372	4.0	3.0
104	SG/APS/ B034/ 31/ 02	பீல்ல வத்த தெருவின் முதல் ஒழுங்கை	154350.511/ 152910.575	154352.063/ 152913.891	154496.07/ 152867.97	154498.125/ 152870.803	3.5	3.0

தொ. இல.	தெருவின் குறியீடு	தெருவின் பெயர்	ஆரம்ப தொகுதி இலக்கங்கள் (கந்தவல இலங்கை)		இறுதித் தொகுதி இலக்கங்கள் (கந்தவல இலங்கை)		பாறை பொது வான நிலம் (மீற்றர்)	பாறை பொது வான அகலம் (மீற்றர்)	அபி விருத்தி அகலம் (மீற்றர்)
			இடம்	வலம்	இடம்	வலம்			
105	SG/ APS/ B034/ 31/ 03	லிந்தபிட்டிய தெரு	154304.71/ 152834.973	154305.897/ 152837.782	154522.292/ 152705.741	154521.95/ 152708.722	364.55	3.0	2.5
106	SG/ APS/ B034/ 31/ 03/ 01	லிந்தபிட்டிய ஆரணிய தெரு	154388.387/ 152674.926	154392.563/ 152675.194	154550.972/ 152553.484	154548.342/ 152555.792	236.12	3.5	2.5
107	SG/ APS/ B034/ 31/ 04	பீல்லவத்த தொடக்கம் கோணபெனிகல வரையிலான தெரு	154275.162/ 152791.666	154274.09/ 152788.334	154205.965/ 152809.811	154206.026/ 152806.312	73.42	3.5	3.0
108	SG/ APS/ B034/ 32	பிம்புர மேல் தோட்டம் ஒற்றையடிப் பாறை	154012.825/ 153424.749	154009.586/ 153424.804	154003.812/ 153644.448	154001.169/ 153645.868	246.52	3.0	2.0
109	SG/ APS/ B034/ 33	அம்பலன்வெல தெரு	153461.878/ 153590.973	153458.194/ 153589.411	153411.402/ 153660.025	153410.345/ 153656.167	116.18	4.0	3.5
110	SG/ APS/ B034/ 34	கோணபெனிகல தெரு	153396.573/ 153201.848	153398.804/ 153204.009	154081.918/ 152867.054	154082.727/ 152869.943	817.68	3.0	2.5
111	SG/ APS/ B034/ 35	ஹேன்யாய தெருவின் முதல் பகுதி	153389.272/ 152995.541	153393.184/ 152998.685	153341.616/ 152602.786	153341.848/ 152598.292	482.11	4.5	4.0
112	SG/ APS/ B034/ 35/ 01	மானகந்த தெரு	153430.222/ 152736.929	153435.079/ 152739.957	154342.32/ 152408.172	154342.144/ 152412.168	1190.05	4.0	3.5

16A

IV (ஈ) கைபெ - ஸ்ரீ லக்ஷ்மீ ப்ரதீபாதி க்ஷத்ரபெ - 2026.01.01

பகுதி IV (ஆ) - இலங்கைச் சனநாயக சோசலிசக் குடியரசு வர்த்தமானப் பத்திரிகை - அதி விசேஷமானது - 2026.01.01

தொ- இல.	தெருவின் குறியீடு	தெருவின் பெயர்	ஆரம்ப தொகுதி இலக்கங்கள் (கந்தவல இலங்கை)		இறுதித் தொகுதி இலக்கங்கள் (கந்தவல இலங்கை)		பாதை பொது வான நீளம் (மீற்றர்)	பாதை பொது வான அகலம் (மீற்றர்)	அபி விருத்தி அகலம் (மீற்றர்)
			இடம்	வலம்	இடம்	வலம்			
113	SG/APS/ B034/ 35/ 01/ 01	மானகந்த தெருவின் முதல் ஒழுங்கை	153899.665/ 152576.357	153895.645/ 152579.514	153984.239/ 152618.235	153981.568/ 152620.496	101.89	3.5	3.0
114	SG/APS/ B034/ 35/ 01/ 02	மானகந்த தெருவின் இரண்டாம் ஒழுங்கை	154039.118/ 152485.79	154036.953/ 152488.545	154106.259/ 152595.084	154104.673/ 152598.204	134.09	3.5	3.0
115	SG/APS/ B034/ 35/ 01/ 03	மானகந்த தெருவின் மூன்றாம் ஒழுங்கை	154041.481/ 152462.55	154041.738/ 152459.016	153662.298/ 152526.853	153659.966/ 152524.243	405.75	3.5	3.0
116	SG/APS/ B034/ 35/ 01/ 04	மானகந்த தெருவின் நான்காம் ஒழுங்கை	154126.013/ 152332.949	154130.983/ 152333.176	154153.784/ 152303.817	154154.445/ 152307.255	48.53	3.5	3.0
117	SG/APS/ B034/ 35/ 02	கும்புருஹை தெரு	153368.378/ 152619.278	153372.246/ 152625.574	153339.415/ 151563.978	153342.627/ 151565.367	1204.47	3.5	3.0
118	SG/APS/ B034/ 36	கிவ்லேஹை தெரு	153305.628/ 153129.141	153306.867/ 153125.338	153206.548/ 152910.147	153210.448/ 152911.03	285.42	4.0	3.0
119	SG/APS/ B034/ 37	கந்தவெல்தொல் தெரு	153249.311/ 153215.57	153252.33/ 153213.785	152981.28/ 152948.11	152983.391/ 152943.015	423.1	3.5	3.0
120	SG/APS/ B034/ 38	ஏழாம் மைல் கம்பம் தொடக்கம் கந்தவெல்தொல் தெரு	153053.703/ 153278.299	153056.199/ 153276.109	152948.854/ 152799.077	152951.034/ 152796.734	1122	3.2	3.0

தொ. இல.	தெருவின் குறியீடு	தெருவின் பெயர்	ஆரம்ப தொகுதி இலக்கங்கள் (கந்தவல இலங்கை)		இறுதித் தொகுதி இலக்கங்கள் (கந்தவல இலங்கை)		பாதை பொது வான நிலம் (மீற்றர்)	பாதை பொது வான அகலம் (மீற்றர்)	அபி விருத்தி அகலம் (மீற்றர்)
			இடம்	வலம்	இடம்	வலம்			
121	SG/ APS/ B034/ 38/ 01	வெடஉன்னஹேன தெரு	152713.194/ 153309.444	152711.435/ 153304.691	152375.237/ 153406.448	152373.893/ 153403.216	366.85	3.5	3.0
122	SG/ APS/ B034/ 38/ 02	டக்கரன்வத்த தெரு	152680.037/ 153166.182	152682.453/ 153163.284	152597.369/ 153144.862	152598.195/ 153141.461	94.28	3.5	3.0
123	SG/ APS/ B034/ 39	எல்லகடே தொடக்கம் பிம்புர வரையிலான தெரு	153159.174/ 153546.815	153157.519/ 153553.13	153482.772/ 153802.755	153479.861/ 153807.714	613.27	4.0	3.6
124	SG/ APS/ B034/ 40	அலுத்தெவத்த தெரு	153010.665/ 153748.025	153009.109/ 153751.891	153219.447/ 153770.356	153216.519/ 153773.082	268.12	4.0	4.0
125	SG/ APS/ B034/ 41	எகொடவத்த தெரு	152952.76/ 153792.175	152954.849/ 153789.182	152590.784/ 154044.446	152595.397/ 154047.95	764.66	3.5	3.0
126	SG/ APS/ B034/ 42	எப்பிட்டவத்த தெரு	152873.971/ 153877.869	152877.218/ 153875.483	152835.639/ 153831.498	152838.333/ 153828.542	65.1	4.0	3.7
127	SG/ APS/ B034/ 43	நிக்ககொட உடவத்த தெரு	152657.431/ 154083.67	152654.879/ 154083.362	152360.208/ 154587.182	152360.132/ 154584.673	713.87	2.5	2.0
128	SG/ APS/ B034/ 44	நிக்ககொட உடும்புர முதல் தெரு	152348.275/ 154207.188	152352.569/ 154205.401	152199.322/ 154093.296	152202.807/ 154092.968	227.71	3.5	2.8

தொ. இல.	தெருவின் குறியீடு	தெருவின் பெயர்	ஆரம்ப தொகுதி இலக்கங்கள் (கந்தவல இலங்கை)		இறுதித் தொகுதி இலக்கங்கள் (கந்தவல இலங்கை)		பாறை பொது வான நிலம் (மீற்றர்)	பாறை பொது வான அகலம் (மீற்றர்)	அபி விருத்தி அகலம் (மீற்றர்)
			இடம்	வலம்	இடம்	வலம்			
137	SG/ APS/ B034/ 48	நிக்ககொட முதல் ஒழுங்கை	151954.285/ 154343.495	151957.929/ 154340.37	151929.476/ 154249.566	151930.281/ 154252.456	221.65	3.0	2.5
138	SG/ APS/ B034/ 49	08 ஏக்கர் எல்லகேடே தோட்டத் தெரு	151611.061/ 154472.237	151614.777/ 154471.403	151773.68/ 154023.63	151774.069/ 154020.655	760.82	3.0	3.0
139	SG/ APS/ B034/ 49/ 01	05 ஏக்கர் இம்புலஹிட்டிஹேன தெரு	151938.098/ 154056.691	151941.446/ 154057.97	151932.947/ 153924.582	151934.081/ 153921.271	182.92	3.5	3.0
140	SG/ APS/ B034/ 50	நிக்ககொட விவசாயப் பண்ணைத் தெரு	151211.374/ 154544.621	151203.484/ 154546.446	151235.423/ 154749.043	151236.685/ 154745.247	436.11	4.0	3.5
141	SG/ APS/ B034/ 51	ஹல்கஹேன தெரு	150926.637/ 154660.74	150923.79/ 154661.863	151152.756/ 154757.59	151154.921/ 154759.668	334.47	3.0	2.8
142	SG/ APS/ B034/ 52	ஹெப்பேவ ஹேன தெரு	150683.495/ 154788.477	150679.725/ 154789.884	150827.894/ 155031.371	150830.496/ 155033.973	730.23	3.7	3.0
143	SG/ APS/ B034/ 52/ 01	ஹெப்பேவ ஹேன தெருவின் முதல் ஒழுங்கை	150621.161/ 155143.169	150617.249/ 155142.86	150647.233/ 155275.072	150643.57/ 155274.726	137.17	3.7	3.0
144	SG/ APS/ B034/ 52/ 02	ஹெப்பேவ ஹேன தெருவின் இரண்டாம் ஒழுங்கை	150789.859/ 155060.569	150786.209/ 155063.43	150892.89/ 155196.562	150889.895/ 155198.701	193.95	3.7	3.0

தொ- இல.	தெருவின் குறியீடு	தெருவின் பெயர்	ஆரம்ப தொகுதி இலக்கங்கள் (கந்தவல இலங்கை)		இறுதித் தொகுதி இலக்கங்கள் (கந்தவல இலங்கை)		பாறை பொது வான அகலம் (மீற்றர்)	அபி விருத்தி அகலம் (மீற்றர்)
			இடம்	வலம்	இடம்	வலம்		
145	SG/APS/ B034/ 53	ஹேன்யாய தெருவின் இரண்டாம் பிரிவு	150599.829/ 154744.569	150604.025/ 154746.216	151605.162/ 153221.781	151608.029/ 153225.251	4.5	4.0
146	SG/APS/ B034/ 53/ 01	ஹேன்யாய தெருவின் இரண்டாம் பிரிவின் முதல் ஒழுங்கை	150901.005/ 154361.832	150897.724/ 154364.184	150941.086/ 154398.682	150937.589/ 154400.624	4.0	3.7
147	SG/APS/ B034/ 53/ 02	ஹேன்யாய தெருவின் இரண்டாம் பிரிவின் இரண்டாம் ஒழுங்கை	150915.379/ 154325.617	150916.725/ 154321.271	150779.801/ 154122.92	150783.759/ 154123.499	4.0	3.5
148	SG/APS/ B034/ 53/ 03	ஹேன்யாய தெருவின் இரண்டாம் பிரிவின் மூன்றாம் ஒழுங்கை	150956.967/ 154236.316	150955.374/ 154240.109	151083.371/ 154306.853	151079.378/ 154307.09	4.0	3.5
149	SG/APS/ B034/ 53/ 04	பொல்வத்த கல்கல் ஹேன்யாய தெரு	151280.724/ 153714.697	151277.754/ 153717.657	151723.026/ 153871.479	151724.304/ 153875.269	4.0	3.6
150	SG/APS/ B034/ 53/ 05	பொல்வத்த கொல்கஹ ஹேன் தெரு	151285.14/ 153710.987	151281.635/ 153713.771	151446.688/ 153665.393	151450.429/ 153666.811	4.0	3.7
151	SG/APS/ B034/ 53/ 06	பொல்வத்த பிரிஸ்ஹேன் தெரு	151566.103/ 153465.149	151565.211/ 153468.661	152196.977/ 153652.594	152193.511/ 153653.566	3.6	3.2
152	SG/APS/ B034/ 53/ 06/ 01	பொல்வத்த பிரிஸ்ஹேன் தெருவின் முதல் ஒழுங்கை	151726.981/ 153602.314	151729.907/ 153603.013	151852.779/ 153438.163	151852.292/ 153441.124	3.0	3.0

தொ. இல.	தெருவின் குறியீடு	தெருவின் பெயர்	ஆரம்ப தொகுதி இலக்கங்கள் (கந்தவல இலங்கை)		இறுதித் தொகுதி இலக்கங்கள் (கந்தவல இலங்கை)		பாதை பொது வான நளம் (மீற்றர்)	பாதை பொது வான அகலம் (மீற்றர்)	அபி விருத்தி அகலம் (மீற்றர்)
			இடம்	வலம்	இடம்	வலம்			
153	SG/ APS/ B034/ 53/ 06/ 02	பொல்வத்த மிரிஸ்லேன தெருவின் இரண்டாம் ஒழுங்கை	151938.141/ 153656.04	151942.147/ 153656.042	151937.134/ 153620.166	151939.911/ 153623.044	37.22	4.0	3.5
154	SG/ APS/ B034/ 53/ 06/ 03	பொல்வத்த மிரிஸ்லேன தெருவின் மூன்றாம் ஒழுங்கை	151953.98/ 153659.429	151958.172/ 153663.244	151999.971/ 153630.358	152002.072/ 153633.762	59.18	4.0	3.5
155	SG/ APS/ B034/ 53/ 06/ 04	பொல்வத்த மிரிஸ்லேன தெருவின் நான்காம் ஒழுங்கை	152047.02/ 153658.921	152043.299/ 153660.465	152055.735/ 153689.167	152052.301/ 153687.115	37.6	4.0	3.7
156	SG/ APS/ B034/ 53/ 07	பொல்வத்த பன்சல தெரு	151594.161/ 153234.354	151588.103/ 153236.539	151564.82/ 153306.85	151560.827/ 153306.625	112.84	4.0	3.5
157	SG/ APS/ B034/ C404/ 01	எல்ல ஓவிட்ட தெரு	160232.449/ 148423.492	160234.269/ 148419.848	160102.703/ 148258.795	160106.689/ 148259.126	274.56	4.0	3.5
158	SG/ APS/ B034/ C404/ 02	அயகம பிரதேச சபைக்கு அருகிலுள்ள தெரு	160277.687/ 148300.551	160275.962/ 148303.6	160360.472/ 148318.25	160361.682/ 148321.535	100.54	3.5	2.5
159	SG/ APS/ B034/ C404/ 03	அயகம கலே பன்சலைத் தெரு	160514.894/ 147862.732	160512.387/ 147864.916	161099.332/ 148315.776	161100.116/ 148318.981	1238.54	3.3	3.3
160	SG/ APS/ B034/ C404/ 04	அயகம கோணபலவத்த தெரு	160664.062/ 147685.186	160661.14/ 147687.992	160692.86/ 147811.045	160690.171/ 147809.713	165.78	3.0	3.0

22A

IV (ஈ) கைபெ - ஸ்ரீ லக்ஷ்மீ பூசாநாதர் சமஸ்தானம் சிவசபை அறிவு - 2026.01.01

பகுதி IV (ஆ) - இலங்கைச் சனநாயக சோசலிசக் குடியரசு வர்த்தமானப் பத்திரிகை - அதி விசேஷமானது - 2026.01.01

தொ. இல.	தெருவின் குறியீடு	தெருவின் பெயர்	ஆரம்ப தொகுதி இலக்கங்கள் (கந்தவல இலங்கை)		இறுதித் தொகுதி இலக்கங்கள் (கந்தவல இலங்கை)		பாதை பொது வான நிலம் (மீற்றர்)	பாதை பொது வான நிலம் (மீற்றர்)	அபிவிருத்தி அகலம் (மீற்றர்)
			இடம்	வலம்	இடம்	வலம்			
161	SG/APS/ B034/ C404/ 05	யக்கஹட்டுவெல பின்னென்ன தெரு	160703.313/ 147661.927	160707.299/ 147661.312	160874.516/ 146570.34	160876.68/ 146573.853	1755.09	4.0	3.5
162	SG/APS/ B034/ C404/ 05/ 01	விட்டோவிட்ட தெரு	160882.102/ 146903.71	160881.546/ 146904.545	160919.215/ 146948.385	160918.248/ 146948.684	62.65	1.0	1.0
163	SG/APS/ B034/ C404/ 05/ 02	யக்கஹட்டுவெல பின்னென்ன ஏ பிரிவு தெருவின் முதல் ஒழுங்கை	160737.493/ 146781.269	160742.01/ 146768.491	160483.043/ 146788.777	160479.708/ 146786.569	313.38	4.0	3.5
164	SG/APS/ B034/ C404/ 06	அமுணுலவிட்ட தெரு	161113.758/ 147357.258	161115.071/ 147355.093	160997.494/ 147284.759	160999.217/ 147282.947	172.08	2.5	2.0
165	SG/APS/ B034/ C404/ 07	பல்லெகட லியன்கஹவந்த தெரு	161319.55/ 147244.647	161317.94/ 147247.179	161595.737/ 147295.555	161595.182/ 147298.504	334.92	3.0	3.0
166	SG/APS/ B034/ C404/ 08	பல்லெகட கலட்டுவகந்த தெரு	161589.331/ 146890.54	161590.577/ 146893.912	163580.055/ 146010.311	163581.573/ 146013.464	2723.02	3.5	3.0
167	SG/APS/ B034/ C404/ 08/ 01	பல்லெகட கலட்டுவகந்த தெருவின் முதல் ஒழுங்கை	161765.24/ 146834.981	161762.385/ 146837.761	162260.645/ 146827.904	162261.944/ 146831.153	592.87	3.5	3.0
168	SG/APS/ B034/ C404/ 08/ 01/ 01	பல்லெகட கலட்டுவகந்த தெருவின் முதல் ஒழுங்கையின் முதல் கிளைவழி	161877.614/ 146942.89	161874.052/ 146943.326	161836.74/ 147058.352	161834.092/ 147056.064	130.08	3.5	3.0

தொ. இல.	தெருவின் குறியீடு	தெருவின் பெயர்	ஆரம்ப தொகுதி இலக்கங்கள் (கந்தவல இலங்கை)		இறுதித் தொகுதி இலக்கங்கள் (கந்தவல இலங்கை)		பாதை பொது வான நீளம் (மீற்றர்)	பாதை பொது வான அகலம் (மீற்றர்)	அபி விருத்தி அகலம் (மீற்றர்)
			இடம்	வலம்	இடம்	வலம்			
169	SG/ APS/ B034/ C404/ 08/ 01/ 02	பல்லெகட கலட்டுவகந்த தெருவின் முதல் ஒழுங்கையின் இரண்டாம் கிளைவழி	162068.884/ 146903.431	162064.528/ 146903.699	162065.967/ 147192.316	162063.483/ 147189.851	363.6	3.5	3.0
170	SG/ APS/ B034/ C404/ 08/ 02	பல்லெகட கலட்டுவகந்த தெருவின் இரண்டாம் ஒழுங்கை	162095.484/ 146610.42	162092.231/ 146612.057	162075.851/ 146720.112	162072.543/ 146718.972	159.95	3.5	3.0
171	SG/ APS/ B034/ C404/ 08/ 03	பல்லெகட கலட்டுவகந்த தெருவின் மூன்றாம் ஒழுங்கை	162235.225/ 146567.227	162231.787/ 146568.616	162277.016/ 146608.193	162274.259/ 146609.377	67.91	3.0	2.5
172	SG/ APS/ B034/ C404/ 08/ 04	பல்லெகட கலட்டுவகந்த தெருவின் நான்காம் ஒழுங்கை	162330.51/ 146539.017	162327.516/ 146539.222	162327.146/ 146639.195	162324.43/ 146637.919	119.75	3.0	2.5
173	SG/ APS/ B034/ C404/ 08/ 05	பல்லெகட கலட்டுவகந்த தெருவின் ஐந்தாம் ஒழுங்கை	162878.678/ 146452.22	162879.894/ 146456.27	162965.425/ 146459.726	162966.543/ 146463.043	113.09	3.5	3.0
174	SG/ APS/ B034/ C404/ 08/ 06	பல்லெகட கலட்டுவகந்த தெருவின் ஆறாம் ஒழுங்கை	163249.055/ 146310.42	163251.852/ 146306.72	163186.802/ 146249.491	163185.128/ 146245.858	101.44	4.0	3.5
175	SG/ APS/ B034/ C404/ 08/ 07	பல்லெகட கலட்டுவகந்த தெருவின் ஏழாம் ஒழுங்கை	163349.292/ 146179.163	163350.69/ 146182.28	163466.236/ 146261.559	163469.087/ 146263.589	210.97	3.5	3.0
176	SG/ APS/ B034/ C404/ 09	பல்லெகட விட்டோவிட்ட தெரு	161542.933/ 146841.653	161545.476/ 146844.786	160870.378/ 146980.519	160869.878/ 146976.55	762.46	4.0	3.0

தொ. இல.	தெருவின் குறியீடு	தெருவின் பெயர்	ஆரம்ப தொகுதி இலக்கங்கள் (கந்தவல இலங்கை)		இறுதித் தொகுதி இலக்கங்கள் (கந்தவல இலங்கை)		பாறை பொது வான அகலம் (மீற்றர்)	பாறை பொது வான அகலம் (மீற்றர்)	அபி விருத்தி அகலம் (மீற்றர்)
			இடம்	வலம்	இடம்	வலம்			
177	SG/APS/ B034/ C404/ 09/ 01	விட்டோவிட்ட பட்டவல தேவாலயத் தெரு	161530.816/ 146859.802	161526.513/ 146860.001	161513.995/ 146908.75	161510.7/ 146906.482	54.77	4.0	3.0
178	SG/APS/ B034/ C404/ 09/ 02	பல்லெகட விட்டோவிட்ட தெருவின் முதல் ஒழுங்கை	161244.901/ 146852.016	161247.853/ 146851.472	161170.512/ 146835.73	161171.291/ 146832.833	88.88	3.0	3.0
179	SG/APS/ B034/ C404/ 10	பல்லெகட கப்புகெவத்த முதல் தெரு	161473.741/ 146680.398	161471.855/ 146677.447	161178.081/ 146730.885	161181.339/ 146729.607	331.29	3.5	3.0
180	SG/APS/ B034/ C404/ 11	பல்லெகட கப்புகெவத்த இரண்டாம் தெரு	161465.864/ 146666.822	161464.162/ 146663.758	161370.433/ 146707.203	161370.628/ 146703.708	112.86	3.5	3.0
181	SG/APS/ B034/ C404/ 12	பல்லெகட கப்புகெவத்த மூன்றாம் தெரு	161319.608/ 146495.3	161318.655/ 146491.334	161145.813/ 146562.262	161144.251/ 146558.58	192.67	4.0	3.5
182	SG/APS/ B034/ C404/ 13	போகஹவங்குவ கிளைப்பாறை	160804.117/ 146384.218	160801.495/ 146382.584	160452.028/ 146512.394	160453.507/ 146509.784	418.81	3.0	3.0
183	SG/APS/ B034/ C404/ 13/ 01	போகஹவெல முதல் ஒழுங்கை	160714.613/ 146378.184	160717.357/ 146376.873	160680.716/ 146305.937	160683.448/ 146304.696	81.59	3.0	3.0
184	SG/APS/ B034/ C404/ 13/ 02	போகஹவெல இரண்டாம் ஒழுங்கை	160663.341/ 146420.705	160665.793/ 146418.821	160614.46/ 146365.428	160615.045/ 146362.485	80.35	3.0	3.0

தொ. இல.	தெருவின் குறியீடு	தெருவின் பெயர்	ஆரம்ப தொகுதி இலக்கங்கள் (கந்தவல இலங்கை)		இறுதித் தொகுதி இலக்கங்கள் (கந்தவல இலங்கை)		பாதை பொது வான நீளம் (மீற்றர்)	பாதை பொது வான அகலம் (மீற்றர்)	அபி விருத்தி அகலம் (மீற்றர்)
			இடம்	வலம்	இடம்	வலம்			
185	SG/ APS/ B034/ C404/ 14	பிட்டகந்த ஓலிவிலகந்த தெரு	160597.821/ 145684.591	160599.598/ 145687.607	160793.718/ 145549.191	160795.465/ 145552.225	245.86	3.5	2.7
186	SG/ APS/ B034/ C404/ 15	பிட்டகந்த மல்கஹேன தெரு	160800.708/ 145218.773	160803.44/ 145216.441	160467.232/ 143887.714	160470.507/ 143889.052	1695.47	3.5	2.5
187	SG/ APS/ B034/ C404/ 15/ 01	பிட்டகந்த மல்கஹேன முதல் ஒழுங்கை	160667.954/ 144809.794	160667.565/ 144806.819	160250.128/ 145116.823	160248.197/ 145114.528	554.23	3.0	3.0
188	SG/ APS/ B034/ C404/ 16	கவரகிரிய முதல் ஒழுங்கை	161128.747/ 144589.87	161128.216/ 144586.652	161049.572/ 144682.218	161046.572/ 144682.209	147.67	3.0	3.0
189	SG/ APS/ B034/ C404/ 17	கவரகிரிய இரண்டாம் ஒழுங்கை	161135.292/ 144579.446	161135.64/ 144582.433	161180.913/ 144512.54	161182.41/ 144515.14	130.99	3.0	3.0
190	SG/ APS/ B034/ C404/ 18	கவரகிரிய மூன்றாம் ஒழுங்கை	161127.88/ 144464.7	161127.449/ 144461.227	161062.547/ 144493.465	161062.922/ 144489.985	77.67	3.5	3.0
191	SG/ APS/ B034/ C404/ 19	கவரகிரிய ரயிகம்கந்த தும்பரமானான தெரு	161779.411/ 143034.835	161779.803/ 143040.087	164105/ 141682.101	164098.104/ 141693.573	2827.95	5.0	2.8
192	SG/ APS/ B034/ C404/ 19/ 01	ரயிகம்கந்த முதல் ஒழுங்கை	162472.51/ 142538.194	162477.055/ 142538.346	162926.879/ 142179.351	162924.239/ 142181.648	598.79	3.5	2.5

தொ. இல.	தெருவின் குறியீடு	தெருவின் பெயர்	ஆரம்ப தொகுதி இலக்கங்கள் (கந்தவல இலங்கை)		இறுதித் தொகுதி இலக்கங்கள் (கந்தவல இலங்கை)		பாதை பொது வான அகலம் (மீற்றர்)	பாதை பொது வான அகலம் (மீற்றர்)	அபி விருத்தி அகலம் (மீற்றர்)
			இடம்	வலம்	இடம்	வலம்			
193	SG/APS/ B034/ C404/ 20	வத்துகாரகம் புலவந்த தெரு	161830.697/ 142377.098	161831.329/ 142372.877	161658.235/ 142284.563	161660.779/ 142281.477	200.13	4.0	2.5
194	SG/APS/ B034/ C404/ 20/ 01	வத்துகாரகம் கல்வந்த தெரு	161770.912/ 142351.185	161767.49/ 142348.967	161407.504/ 142626.852	161406.567/ 142622.963	484.68	4.0	2.5
195	SG/APS/ B034/ C404/ 21	வத்துகாரகம் எகிரிகனத்த தெரு	161854.188/ 142336.153	161857.671/ 142334.179	162065.157/ 142085.338	162069.155/ 142085.488	465.95	4.0	2.5
196	SG/APS/ B034/ C404/ 21/ 01	வத்துகாரகம் எகிரிகனத்த தெருவின் முதல் ஒழுங்கை	161853.994/ 142265.949	161857.565/ 142259.677	161772.003/ 142238.716	161770.111/ 142236.387	210.73	3.0	2.5
197	SG/APS/ B034/ C404/ 22	வத்துகாரகம் தொரலபிட்டிய தெரு	162332.269/ 142015.546	162336.192/ 142013.515	162224.993/ 141974.511	162227.987/ 141971.858	124.22	4.0	3.0
198	SG/APS/ B034/ C404/ D405/ 01	பல்லெகட வெலிகடவந்த தெரு	161844.513/ 146592.528	161847.643/ 146590.71	161750.31/ 146468.354	161753.01/ 146467.049	233.54	3.0	2.0
199	SG/APS/ B034/ C404/ D405/ 02	பல்லெகட கமிக்கந்த முதல் ஒழுங்கை	162037.316/ 146402.471	162040.726/ 146400.334	162174.399/ 145975.895	162175.937/ 145979.587	563.2	4.0	2.7
200	SG/APS/ B034/ C404/ D405/ 03	பல்லெகட கமிக்கந்த இரண்டாம் ஒழுங்கை	162453.292/ 146174.872	162456.176/ 146173.464	162428.868/ 145826.889	162431.61/ 145825.195	399.09	3.0	2.5

தொ. இல.	தெருவின் குறியீடு	தெருவின் பெயர்	ஆரம்ப தொகுதி இலக்கங்கள் (கந்தவல இலங்கை)		இறுதித் தொகுதி இலக்கங்கள் (கந்தவல இலங்கை)		பாறை பொது வான நிலம் (மீற்றர்)	பாறை பொது வான நிலம் (மீற்றர்)	அபி விருத்தி அகலம் (மீற்றர்)
			இடம்	வலம்	இடம்	வலம்			
201	SG/ APS/ B034/ C404/ D405/ 04	பல்லெகட கலட்டுவகந்த முதல் ஒழுங்கை	162474.041/ 146170.034	162470.718/ 146171.919	162504.53/ 146482.959	162500.934/ 146484.458	488.03	3.8	3.0
202	SG/ APS/ B034/ C404/ D405/ 05	பல்லெகட கலட்டுவகந்த இரண்டாம் ஒழுங்கை ஒற்றையடிப்பாறை	162686.261/ 146095.816	162683.748/ 146096.055	162811.398/ 146422.064	162808.898/ 146422.148	478.88	2.5	1.0
203	SG/ APS/ B034/ C404/ D405/ 06	கங்கொடகந்த மெல்கொடெல்ல தெரு	162968.06/ 145953.49	162965.454/ 145954.98	163006.478/ 146187.935	163003.508/ 146188.359	262.04	3.0	2.6
204	SG/ APS/ B034/ C404/ D405/ 07	கங்கொடகந்த 60 ஏக்கர் கலட்டுவகந்த தெரு	163512.077/ 145858.981	163508.787/ 145861.253	163471.577/ 146000.074	163469.503/ 145995.972	176.79	3.0	2.0
205	SG/ APS/ B034/ C404/ D405/ 08	வட்டகுருகல தெரு	163588.386/ 145811.609	163591.924/ 145808.958	164489.39/ 144732.269	164490.466/ 144736.122	1968.75	4.0	3.3
206	SG/ APS/ B034/ C404/ D405/ 08/ 01	வட்டகுருகல ஹென்யாய தெரு	163566.841/ 145755.912	163568.726/ 145759.463	163965.736/ 145418.686	163968.755/ 145414.624	645.72	4.0	3.5
207	SG/ APS/ B034/ C404/ D405/ 08/ 02	எல்லவிட்ட ஹென்யாய தெரு	163496.965/ 145572.992	163499.761/ 145569.916	163253.998/ 145287.284	163257.699/ 145288.802	628.02	4.0	3.5
208	SG/ APS/ B034/ C404/ D405/ 08/ 03	கெட்டக்கெரெல்ல ஹென்யாய தெரு	163616.035/ 145268.563	163613.876/ 145271.966	164357.348/ 145066.841	164354.49/ 145069.726	961.49	4.0	3.5

தொ. இல.	தெருவின் குறியீடு	தெருவின் பெயர்	ஆரம்ப தொகுதி இலக்கங்கள் (கந்தவல இலங்கை)		இறுதித் தொகுதி இலக்கங்கள் (கந்தவல இலங்கை)		பாதை பொது வான அகலம் (மீற்றர்)	பாதை பொது வான அகலம் (மீற்றர்)	அபி விருத்தி அகலம் (மீற்றர்)
			இடம்	வலம்	இடம்	வலம்			
209	SG/APS/ B034/ C404/ D405/ 08/ 03/ 01	ஹென்யாய் கெட்டக்கொல்ல கீழ் தெரு	163990.074/ 145237.543	163987.423/ 145240.036	163851.196/ 145487.983	163851.066/ 145484.486	364.15	3.5	2.5
210	SG/APS/ B034/ C404/ D405/ 09	36 ஏக்கர் முதல் ஒழுங்கை	163800.119/ 145712.003	163797.125/ 145714.771	164706.8/ 145736.521	164709.94/ 145738.999	1311.94	4.0	3.5
211	SG/APS/ B034/ C404/ D405/ 10	36 ஏக்கர் இரண்டாம் ஒழுங்கை	164021.24/ 145639.8	164017.23/ 145641.462	163951.793/ 145849.01	163947.772/ 145849.286	415.39	4.0	3.5
212	SG/APS/ B034/ C404/ D405/ 11	பதுவலகந்த கல்கெரெந்த தெரு	165014.641/ 145280.167	165015.231/ 145284.137	165346.832/ 145401.242	165346.488/ 145405.227	431.27	4.0	3.5
213	SG/APS/ B034/ C404/ D405/ 11/ 01	கல்கெரெந்த கலத்தூர தெரு	165158.3/ 145353.973	165152.821/ 145351.331	166198.582/ 145939.273	166195.509/ 145937.524	1493.54	3.0	2.5
214	SG/APS/ B034/ C404/ D405/ 12	பதுவலகந்த 100 ஏக்கர் கிளைப் பாதை	165015.18/ 145244.641	165017.981/ 145242.209	165068.311/ 145044.802	165069.977/ 145046.032	223.49	2.0	1.0
215	SG/APS/ B034/ C404/ D408/ 01	லபுளலேறென தெரு	160521.458/ 145830.534	160525.82/ 145828.924	160432.723/ 145663.672	160436.722/ 145663.788	281.21	4.0	3.5
216	SG/APS/ B034/ C404/ D408/ 02	தேயிலைக் குடியேற்றம் மஹிந்தாராம தெரு	160446.711/ 145882.744	160442.926/ 145885.192	160619.012/ 146203.898	160615.756/ 146202.615	457.76	3.5	3.0

தொ. இல.	தெருவின் குறியீடு	தெருவின் பெயர்	ஆரம்ப தொகுதி இலக்கங்கள் (கந்தவல இலங்கை)		இறுதித் தொகுதி இலக்கங்கள் (கந்தவல இலங்கை)		பாறை பொது வான நிலம் (மீற்றர்)	பாறை பொது வான அகலம் (மீற்றர்)	அபி விருத்தி அகலம் (மீற்றர்)
			இடம்	வலம்	இடம்	வலம்			
217	SG/ APS/ B034/ C404/ D408/ 02/ 01	தேயிலைக் குடியேற்றம் மஹிந்தாராமய தெருவின் முதல் ஒழுங்கை	160442.851/ 145922.735	160442.156/ 145926.425	160483.797/ 145913.543	160481.311/ 145916.511	47.94	3.5	3.0
218	SG/ APS/ B034/ C404/ D408/ 02/ 02	தேயிலைக் குடியேற்றம் மஹிந்தாராமய தெருவின் இரண்டாம் ஒழுங்கை	160436.421/ 145971.767	160435.934/ 145975.38	160544.63/ 145900.79	160546.658/ 145903.644	169.64	3.5	3.0
219	SG/ APS/ B034/ C404/ D408/ 02/ 02/ 01	தேயிலைக் குடியேற்றம் மஹிந்தாராமய தெருவின் இரண்டாம் ஒழுங்கையின் முதல் கிணைப்பாறை	160483.556/ 145920.016	160481.336/ 145924.6	160511.205/ 145979.264	160508.558/ 145977.853	77.25	3.0	2.0
220	SG/ APS/ B034/ C404/ D408/ 02/ 03	தேயிலைக் குடியேற்றம் மஹிந்தாராமய தெருவின் மூன்றாம் ஒழுங்கை	160497.179/ 146104.457	160502.297/ 146106.814	160622.966/ 146038.814	160623.854/ 146042.199	157.01	3.5	3.0
221	SG/ APS/ B034/ C404/ D408/ 02/ 04	தேயிலைக் குடியேற்றம் மஹிந்தாராமய தெருவின் நான்காம் ஒழுங்கை	160613.368/ 146186.927	160617.507/ 146187.826	160787.105/ 146149.908	160786.575/ 146153.368	189.6	3.5	3.0
222	SG/ APS/ B034/ C404/ D408/ 03	மஹிந்தாராமய முதல் ஒழுங்கை	160355.127/ 146027.079	160352.312/ 146029.781	160402.833/ 146058.487	160403.62/ 146061.383	77.36	3.0	3.0
223	SG/ APS/ B034/ C404/ D408/ 04	ஹேவாஹெட்ட சமகி மாவத்தை	160333.715/ 146026.165	160330.912/ 146023.308	159539.665/ 146365.582	159545.419/ 146358.971	1699.38	4.0	3.0
224	SG/ APS/ B034/ C404/ D408/ 04/ 01	ஹேவாஹெட்ட சமகி மாவத்தையின் முதல் ஒழுங்கை	159844.226/ 146691.312	159841.171/ 146691.491	160035.912/ 146800.095	160032.973/ 146800.693	280.25	3.0	2.5

தொ. இல.	தெருவின் குறியீடு	தெருவின் பெயர்	ஆரம்ப தொகுதி இலக்கங்கள் (கந்தவல இலங்கை)		இறுதித் தொகுதி இலக்கங்கள் (கந்தவல இலங்கை)		பாறை பொது வான நிலம் (மீற்றர்)	பாறை பொது வான நிலம் (மீற்றர்)	அபி விருத்தி அகலம் (மீற்றர்)
			இடம்	வலம்	இடம்	வலம்			
225	SG/APS/ B034/ C404/ D408/ 04/ 01/ 01	ஹேவாஹெட்ட சமகி மாவத்தையின் முதல் ஒழுங்கையின் முதல் கிளைத்தெரு	159861.741/ 146731.182	159857.518/ 146729.35	159889.727/ 146770.212	159887.787/ 146770.695	54.14	2.0	2.0
226	SG/APS/ B034/ C404/ D408/ 04/ 02	ஹேவாஹெட்ட சமகி மாவத்தையின் இரண்டாம் ஒழுங்கை	159728.552/ 146728.858	159724.349/ 146728.619	159621.929/ 146975.422	159618.476/ 146973.403	477.04	4.0	3.0
227	SG/APS/ B034/ C404/ D408/ 04/ 02/ 01	ஹேவாஹெட்ட சமகி மாவத்தையின் இரண்டாம் ஒழுங்கை முதல் கிளைத்தெரு - ஒற்றையடிப் பாறை	159684.662/ 146936.945	159685.741/ 146936.62	159659.818/ 146854.201	159660.429/ 146853.41	114.3	1.0	1.0
228	SG/APS/ B034/ C404/ D408/ 04/ 03	நயதேகல் பன்சலைத் தெரு	159527.537/ 146619.396	159528.152/ 146616.423	159454.032/ 146835.225	159452.04/ 146837.468	272.6	3.0	3.0
229	SG/APS/ B034/ C404/ D408/ 05	தேயிலைக் குடியேற்றம் மாளெஸ் மாவத்தை	160127.361/ 145996.403	160136.435/ 145993.731	159972.445/ 145325.07	159976.308/ 145326.109	1066.31	4.0	3.0
230	SG/APS/ B034/ C404/ D408/ 06	பிட்டகந்த தேயிலைக் குடியேற்றத் தெருவின் முதல் ஒழுங்கை	159935.545/ 146138.611	159931.765/ 146137.118	160021.294/ 146332.061	160017.931/ 146334.367	237.03	4.0	3.0
231	SG/APS/ B034/ C404/ D408/ 07	பிட்டகந்த தேயிலைக் குடியேற்றத் தெருவின் இரண்டாம்; ஒழுங்கை	159904.209/ 146054.641	159908.641/ 146056.417	159969.111/ 146013.315	159972.1/ 146015.971	80.33	4.0	3.0
232	SG/APS/ B034/ C404/ D408/ 08	பேரகஹ வளைவு உட்பட்ட தெரு	159857.111/ 146242.784	159853.795/ 146244.029	159711.282/ 146499.991	159709.728/ 146496.855	358.11	3.5	2.5

தொ. இல.	தெருவின் குறியீடு	தெருவின் பெயர்	ஆரம்ப தொகுதி இலக்கங்கள் (கந்தவல இலங்கை)		இறுதித் தொகுதி இலக்கங்கள் (கந்தவல இலங்கை)		பாதை பொது வான நீளம் (மீற்றர்)	பாதை பொது வான அகலம் (மீற்றர்)	அபி விருத்தி அகலம் (மீற்றர்)
			இடம்	வலம்	இடம்	வலம்			
233	SG/ APS/ B034/ C404/ D408/ 09	தேயிலைக் குடியேற்றம் திவிகல்பொத்த தெரு	159460.488/ 146382.954	159464.417/ 146384.485	159785.131/ 145677.525	159788.05/ 145679.456	987.55	3.5	2.5
234	SG/ APS/ B034/ C404/ D408/ 10	தேயிலைக் குடியேற்றம் பட்டேறன தெரு	159381.228/ 146257.082	159383.543/ 146259.709	158653.716/ 145864.021	158653.703/ 145860.52	1088	3.5	2.5
235	SG/ APS/ B034/ C404/ D408/ 10/ 01	தேயிலைக் குடியேற்றம் பட்டேறன தெருவின் முதல் ஒழுங்கை	159023.381/ 145826.412	159026.802/ 145825.655	159031.943/ 145705.343	159035.056/ 145703.743	128.99	3.5	2.5
236	SG/ APS/ B034/ C404/ D408/ 10/ 02	பட்டேறன கங்கபடதென்ன தெரு	158823.117/ 145833.604	158827.38/ 145833.628	157898.987/ 146369.526	157897.891/ 146365.679	1281.97	4.0	2.5
237	SG/ APS/ B034/ C404/ D408/ 10/ 02/ 01	பட்டேறன கங்கபடதென்ன தெருவின் முதல் ஒழுங்கை	158123.941/ 146033.877	158126.979/ 146032.992	158118.056/ 145966	158120.711/ 145967.398	71.9	3.0	2.5
238	SG/ APS/ B034/ C404/ D408/ 10/ 03	பட்டேறன பன்விலதென்ன தெரு	158665.833/ 145861.996	158662.019/ 145863.469	158452.434/ 146279.232	158454.773/ 146275.988	640.35	4.0	3.0
239	SG/ APS/ B034/ C404/ D408/ 11	தேயிலைக் குடியேற்றம் நாமண்டிய தெரு	159260.484/ 146291.527	159260.331/ 146287.138	159027.237/ 146166.165	159026.768/ 146162.697	348.73	3.5	2.5
240	SG/ APS/ B034/ C404/ D408/ 12	கந்துருவந்தொல கலபல்ல தெரு	159290.047/ 146758.405	159287.228/ 146760.688	160057.767/ 147501.851	160054.738/ 147503.62	1411.76	3.5	2.5

32A

IV (ஈ) கைபெ - ஸ்ரீ லக்ஷ்மீ பூசாநாதர் சமஸ்தான ஸ்ரீ லக்ஷ்மீ பூசாநாதர் - 2026.01.01

பகுதி IV (ஆ) - இலங்கைச் சனநாயக சோசலிசக் குடியரசு வர்த்தமானப் பத்திரிகை - அதி விசேஷமானது - 2026.01.01

தொ. இல.	தெருவின் குறியீடு	தெருவின் பெயர்	ஆரம்ப தொகுதி இலக்கங்கள் (கந்தவல இலங்கை)		இறுதித் தொகுதி இலக்கங்கள் (கந்தவல இலங்கை)		பாறை பொது வான அகலம் (மீற்றர்)	பாறை பொது வான அகலம் (மீற்றர்)	அபி விருத்தி அகலம் (மீற்றர்)
			இடம்	வலம்	இடம்	வலம்			
241	SG/APS/ B034/ C404/ D408/ 13	பிட்டகந்த தெம்புகல்பொத்த கிராம சபைத் தெரு	158992.757/ 146918.043	158988.008/ 146924.988	159832.598/ 147571.895	159828.886/ 147573.398	4.0	4.0	2.0
242	SG/APS/ B034/ C404/ D408/ 14	பிட்டகந்த தலபத்கல கெந்தகல தெரு	158955.393/ 146975.354	158951.401/ 146974.973	156821.817/ 149321.023	156824.14/ 149317.398	4.0	4.0	2.8
243	SG/APS/ B034/ C404/ D408/ 14/ 01	பிட்டகந்த தலபத்கல தெரு	158841.061/ 147045.431	158837.28/ 147049.861	158171.437/ 147818.672	158172.122/ 147814.73	4.0	4.0	2.5
244	SG/APS/ B034/ C404/ D408/ 14/ 02	பிட்டகந்த தலபத்கல தெருவின் முதல் ஒழுங்கை	157498.96/ 147878.859	157499.586/ 147874.677	157234.824/ 148089.31	157231.423/ 148087.205	4.0	4.0	2.5
245	SG/APS/ B034/ C404/ D408/ 15	பிட்டகந்த முதல் ஒழுங்கை - ஒற்றையடிப் பாறை	158952.29/ 146786.431	158950.896/ 146783.128	158653.804/ 146783.737	158655.668/ 146779.791	3.0	3.0	2.6
246	SG/APS/ B034/ C404/ D408/ 16	பிட்டகந்த பன்விலதென்ன தெரு	158992.752/ 146695.263	158995.733/ 146698.178	158585.268/ 146197.093	158584.856/ 146193.067	4.0	4.0	3.0
247	SG/APS/ B034/ C404/ D408/ 17	பிட்டகந்த தெருவின் இரண்டாம் ஒழுங்கை	158938.103/ 146697.138	158942.203/ 146696.806	158961.325/ 146672.98	158964.134/ 146674.035	3.0	3.0	2.6
248	SG/APS/ B034/ C404/ D408/ 18	பிட்டகந்த தெருவின் மூன்றாம் ஒழுங்கை	158527.876/ 146838.288	158530.889/ 146838.527	158516.682/ 146572.202	158517.281/ 146575.142	3.0	3.0	2.5

தொ. இல.	தெருவின் குறியீடு	தெருவின் பெயர்	ஆரம்ப தொகுதி இலக்கங்கள் (கந்தவல இலங்கை)		இறுதித் தொகுதி இலக்கங்கள் (கந்தவல இலங்கை)		பாறை பொது வான நிலம் (மீற்றர்)	பாறை பொது வான நிலம் (மீற்றர்)	அபி விருத்தி அகலம் (மீற்றர்)
			இடம்	வலம்	இடம்	வலம்			
249	SG/ APS/ B034/ C404/ D408/ 19	பிட்டகந்த தெருவின் நான்காம் ஒழுங்கை	158391.624/ 146794.043	158394.664/ 146793.94	158383.118/ 146734.843	158383.936/ 146731.956	68.16	3.0	2.6
250	SG/ APS/ B034/ C404/ D408/ 20	பிட்டகந்த தெருவின் ஐந்தாம் ஒழுங்கை	158371.028/ 146839.404	158370.205/ 146841.229	158389.514/ 146863.734	158387.878/ 146864.886	33.99	2.0	1.6
251	SG/ APS/ B034/ C404/ D408/ 21	பிட்டகந்த தெருவின் ஆறாம் ஒழுங்கை	158320.446/ 146865.636	158314.122/ 146867.684	157949.878/ 146559.532	157951.843/ 146556.634	1178.49	3.5	3.0
252	SG/ APS/ B034/ C404/ D408/ 21/ 01	பிட்டகந்த தெருவின் ஆறாம் ஒழுங்கையின் முதல் கிளைத் தெரு - ஒற்றையடிப் பாதை	157801.663/ 147049.828	157798.386/ 147047.874	157712.91/ 147152.417	157710.026/ 147153.239	165.53	3.0	2.5
253	SG/ APS/ B034/ C404/ D408/ 22	பிட்டகந்த கிராம சபை ஒற்றையடிப்பாதை	158185.44/ 146770.019	158188.761/ 146770.059	157934.147/ 146347.428	157935.373/ 146343.932	545.86	3.0	1.6
254	SG/ APS/ B034/ C404/ D408/ 23	பிட்டகந்த தெருவின் ஏழாம் ஒழுங்கை	158184.025/ 146774.431	158185.44/ 146770.019	157856.121/ 146923.467	157860.114/ 146923.231	434.81	4.0	1.0
255	SG/ APS/ B034/ C404/ D406/ 01	மா மரச் சந்தி கலுமெதிரிய தெரு	161131.443/ 145171.071	161134.896/ 145173.252	162750.019/ 144418.317	162752.289/ 144421.611	2582.81	4.0	3.0
256	SG/ APS/ B034/ C404/ D406/ 01/ 01	கலுமெதிரிய தெருவின் முதல் ஒழுங்கை	162224.666/ 144453.272	162227.802/ 144450.355	162240.579/ 144363.174	162241.403/ 144366.058	103.38	3.0	2.5

தொ. இல.	தெருவின் குறியீடு	தெருவின் பெயர்	ஆரம்ப தொகுதி இலக்கங்கள் (கந்தவல இலங்கை)		இறுதித் தொகுதி இலக்கங்கள் (கந்தவல இலங்கை)		பாதை பொது வான அகலம் (மீற்றர்)	பாதை பொது வான அகலம் (மீற்றர்)	அபி விருத்தி அகலம் (மீற்றர்)
			இடம்	வலம்	இடம்	வலம்			
257	SG/APS/ B034/ C404/ D406/ 01/ 02	கலுமெதிரிய தேயிலை மலை குட்டிகந்த தெரு	162264.039/ 144484.394	162260.383/ 144487.966	164605.873/ 142928.664	164610.047/ 142928.024	3867.5	4.0	3.0
258	SG/APS/ B034/ C404/ D406/ 01/ 02/ 01	கலுமெதிரிய தேயிலை மலை குட்டிகந்த தெருவின் முதல் ஒழுங்கை	164581.481/ 143010.128	164579.459/ 143013.662	164648.764/ 143122.174	164646.671/ 143125.582	137.74	4.0	3.0
259	SG/APS/ B034/ C404/ D406/ 01/ 03	கலுமெதிரிய தெருவின் இரண்டாம் ஒழுங்கை	162112.541/ 144752.893	162110.722/ 144749.256	161559.35/ 145069.992	161557.014/ 145066.745	667.89	4.0	3.5
260	SG/APS/ B034/ C404/ D406/ 01/ 04	கலுமெதிரிய தெருவின் மூன்றாம் ஒழுங்கை	162123.865/ 144753.511	162126.766/ 144755.492	162212.608/ 144716.623	162213.008/ 144720.099	99.83	3.5	3.0
261	SG/APS/ B034/ C404/ D406/ 01/ 05	கலுமெதிரிய தெருவின் நான்காம் ஒழுங்கை	162370.841/ 144695.009	162366.643/ 144697.738	162578.124/ 144642.282	162581.031/ 144644.23	244.7	3.5	3.0
262	SG/APS/ B034/ C404/ D406/ 02	மா மரச் சந்தி கிராம சபைத் தெரு	161135.019/ 145178.676	161132.62/ 145175.212	161022.205/ 145644.805	161019.354/ 145641.999	557.3	4.0	2.5
263	SG/APS/ B034/ C404/ D406/ 03	ஹெரெஸ்ஸ கமிக்கந்தவத்த தெரு	161605.18/ 145371.611	161608.64/ 145371.892	162768.247/ 144927.2	162765.285/ 144927.678	1417.51	3.0	2.5
264	SG/APS/ B034/ C404/ D406/ 03/ 01	ஹெரெஸ்ஸ கமிக்கந்தவத்த தெருவின் முதல் ஒழுங்கை	161723.374/ 145276.48	161725.7/ 145273.754	161612.773/ 145238.659	161612.75/ 145235.159	125.73	3.5	3.0

தொ. இல.	தெருவின் குறியீடு	தெருவின் பெயர்	ஆரம்ப தொகுதி இலக்கங்கள் (கந்தவல இலங்கை)		இறுதித் தொகுதி இலக்கங்கள் (கந்தவல இலங்கை)		பாறை பொது வான நீளம் (மீற்றர்)	பாறை பொது வான அகலம் (மீற்றர்)	அபி விருத்தி அகலம் (மீற்றர்)
			இடம்	வலம்	இடம்	வலம்			
265	SG/ APS/ B034/ C404/ D406/ 03/ 02	ஹெரெஸ்ஸ கமிக்கந்தவத்த கலுமெதிரிய தெரு	162368.317/ 144896.297	162375.609/ 144893.679	162499.257/ 144666.71	162502.681/ 144664.757	298.32	3.5	2.0
266	SG/ APS/ B034/ C404/ D406/ 04	திக்கல ஹெரெஸ்ஸ முதல் ஒழுங்கை	161757.972/ 145517.095	161753.657/ 145517.637	161631.558/ 145673.812	161634.352/ 145672.721	324.09	3.0	2.5
267	SG/ APS/ B034/ C404/ D406/ 05	திக்கல ஹெரெஸ்ஸ இரண்டாம் ஒழுங்கை	161830.27/ 145488.7	161827.098/ 145490.218	161859.82/ 145549.14	161857.127/ 145551.377	70.26	3.5	3.0
268	SG/ APS/ B034/ C404/ D406/ 06	திக்கல ஹெரெஸ்ஸ மூன்றாம் ஒழுங்கை	162188.258/ 145563.453	162185.755/ 145561.775	161942.929/ 145692.707	161939.989/ 145693.305	307	3.0	2.5
269	SG/ APS/ B034/ C404/ D406/ 07	கமிக்கந்த பல்லெகட தெரு	162742.986/ 145275.341	162740.918/ 145278.928	162286.339/ 145870.993	162287.869/ 145867.297	976.53	4.0	3.0
270	SG/ APS/ B034/ C404/ D406/ 07/ 01	கமிக்கந்த பல்லெகட தெருவின் முதல் ஒழுங்கை	162807.26/ 145344.143	162810.308/ 145346.885	162934.139/ 145311.753	162930.158/ 145312.137	163.63	4.0	2.5
271	SG/ APS/ B034/ C404/ D406/ 08	ஹெரெஸ்ஸ 20 ஏக்கர் தெரு	162781.233/ 145178.911	162783.57/ 145175.794	163371.974/ 144353.077	163372.966/ 144350.245	1227.93	3.0	2.5
272	SG/ APS/ B034/ C404/ D406/ 08/ 01	ஹெரெஸ்ஸ 20 ஏக்கர் கல்பொத்த தெரு	163169.07/ 144636.912	163172.194/ 144635.587	163154.466/ 144365.837	163156.867/ 144367.636	449.28	3.0	2.5

36A

IV (ஈ) கைபெ - ஸ்ரீ லக்ஷ்மீ பூசாநாதர் சமஸ்தானம் ஸ்ரீ லக்ஷ்மீ பூசாநாதர் - 2026.01.01

பகுதி IV (ஆ) - இலங்கைச் சனநாயக சோசலிசக் குடியரசு வர்த்தமானப் பத்திரிகை - அதி விசேஷமானது - 2026.01.01

தொ. இல.	தெருவின் குறியீடு	தெருவின் பெயர்	ஆரம்ப தொகுதி இலக்கங்கள் (கந்தவல இலங்கை)		இறுதித் தொகுதி இலக்கங்கள் (கந்தவல இலங்கை)		பாறை பொது வான அகலம் (மீற்றர்)	பாறை பொது வான அகலம் (மீற்றர்)	அபி விருத்தி அகலம் (மீற்றர்)
			இடம்	வலம்	இடம்	வலம்			
273	SG/APS/ B034/ C404/ D406/ 09	திக்கல ஹெரெஸ்ஸ தெரு	162982.034/ 145043.287	162978.825/ 145045.674	163923.35/ 144979.121	163920.473/ 144982.068	4.0	3.0	
274	SG/APS/ B034/ C404/ D406/ 09/ 01	திக்கல மூக்கலான தெரு	163169.314/ 145100.199	163169.314/ 145100.199	163056.984/ 145390.869	163054.742/ 145388.875	3.0	2.0	
275	SG/APS/ B034/ C404/ D406/ 10	திக்கல ஹெரெஸ்ஸ நான்காம் ஒழுங்கை	163495.456/ 144665.743	163490.517/ 144667.758	163580.059/ 144758.336	163580.113/ 144761.836	3.5	2.5	
276	SG/APS/ B034/ C404/ D406/ 11	திக்கல ஹெரெஸ்ஸ கிளைப்பாறை - ஒற்றையடிப் பாறை	163662.368/ 144590.539	163660.819/ 144591.402	163837.071/ 144889.362	163836.118/ 144888.003	1.5	1.0	
277	SG/APS/ B034/ C404/ D406/ 12	குட்டிகந்த தெரு	163664.449/ 144585.944	163667.172/ 144584.426	164044.067/ 144246.188	164044.113/ 144249.187	3.0	3.0	
278	SG/APS/ B034/ C404/ D406/ 12/ 01	குட்டிகந்த உமங்க்தொல தெரு	163639.496/ 144482.403	163639.278/ 144479.904	163494.483/ 144343.5	163496.523/ 144344.945	2.5	2.0	
279	SG/APS/ B034/ C404/ D407/ 01	கவரகிரிய வயல் பாறை ஊடாக முனிவரின் கந்த தெரு முதல் ஒழுங்கை	160699.858/ 143935.506	160703.361/ 143935.567	160661.878/ 143848.602	160664.132/ 143845.925	3.5	3.0	
280	SG/APS/ B034/ C404/ D407/ 02	கவரகிரிய கொலம்பேவ தெரு	160327.199/ 143850.242	160329.754/ 143845.734	158174.679/ 143543.167	158176.11/ 143540.53	3.0	2.8	

தொ. இல.	தெருவின் குறியீடு	தெருவின் பெயர்	ஆரம்ப தொகுதி இலக்கங்கள் (கந்தவல இலங்கை)		இறுதித் தொகுதி இலக்கங்கள் (கந்தவல இலங்கை)		பாதை பொது வான நிலம் (மீற்றர்)	பாதை பொது வான அகலம் (மீற்றர்)	அபி விருத்தி அகலம் (மீற்றர்)
			இடம்	வலம்	இடம்	வலம்			
281	SG/ APS/ B034/ C404/ D407/ 02/ 01	கம்வசம முதல் ஒழுங்கை	160148.25/ 143158.168	160149.739/ 143161.848	160251.028/ 143076.245	160254.979/ 143076.863	140.62	4.0	3.0
282	SG/ APS/ B034/ C404/ D407/ 02/ 02	நேபடகந்த தெரு	159992.397/ 143096.675	159988.046/ 143097.569	158432.198/ 143398.985	158433.316/ 143395.136	2083.16	4.0	3.0
283	SG/ APS/ B034/ C404/ D407/ 02/ 02/ 01	கொந்தகல தெரு	158669.768/ 143759.738	158673.128/ 143762.179	158169.001/ 143726.865	158173.893/ 143724.586	1119.83	4.0	3.0
284	SG/ APS/ B034/ C404/ D407/ 02/ 02/ 02	நேபடகந்த தெருவின் முதல் ஒழுங்கை	158454.333/ 143404.292	158459.596/ 143408.227	158565.735/ 143409.54	158564.696/ 143413.403	113.2	4.0	3.0
285	SG/ APS/ B034/ C404/ D407/ 02/ 03	நிக்கஹ புலத்திங்ஹல தெரு	159860.232/ 142810.67	159869.03/ 142810.453	160719.397/ 142209.444	160720.446/ 142213.304	1113.02	4.0	3.0
286	SG/ APS/ B034/ C404/ D407/ 02/ 03/ 01	நிக்கஹ புலத்திங்ஹல தெருவின் முதல் ஒழுங்கை	160588.267/ 142272.567	160586.011/ 142274.583	160721.102/ 142641.984	160721.439/ 142644.966	924.49	3.0	2.6
287	SG/ APS/ B034/ C404/ D407/ 02/ 04	கம்வசம போதி நேபடகந்த தெரு	159758.823/ 142781.741	159754.918/ 142780.886	159730.077/ 143276.113	159727.642/ 143278.002	1077.1	3.0	3.0
288	SG/ APS/ B034/ C404/ D407/ 02/ 05	கவரகிரிய கொலம்பேவ தெருவின் முதல் ஒழுங்கை	159720.815/ 142722.739	159720.174/ 142719.347	159357.438/ 142973.765	159359.763/ 142971.87	515.98	3.0	2.7

38A

IV (ஈ) கைபெ - ஐ லெகா பூசுநாந்நிகு ஸலாபலாடி ப்நரபயே டிதி பிலேஷ டுபபி ப்நுய - 2026.01.01

பகுதி IV (ஆ) - இலங்கைச் சனநாயக சோசலிசக் குடியரசு வர்த்தமானப் பத்திரிகை - அதி விசேஷமானது - 2026.01.01

தொ. இல.	தெருவின் குறியீடு	தெருவின் பெயர்	ஆரம்ப தொகுதி இலக்கங்கள் (கந்தவல இலங்கை)		இறுதித் தொகுதி இலக்கங்கள் (கந்தவல இலங்கை)		பாறை பொது வான நிலம் (மீற்றர்)	பாறை பொது வான அகலம் (மீற்றர்)	அபி விருத்தி அகலம் (மீற்றர்)
			இடம்	வலம்	இடம்	வலம்			
289	SG/APS/ B034/ C404/ D407/ 02/ 06	கவரகிரிய கொலம்பேவ தெருவின் இரண்டாம் ஒழுங்கை	158383.129/ 143228.229	158383.713/ 143232.571	158576.865/ 143284.811	158574.171/ 143288.034	237.37	4.2	2.8
290	SG/APS/ B034/ C404/ D407/ 02/ 07	கவரகிரிய கொலம்பேவ தெருவின் மூன்றாம் ஒழுங்கை	158282.665/ 143540.767	158278.032/ 143541.949	158197.617/ 144086.884	158196.338/ 144089.597	652.69	3.0	3.0
291	SG/APS/ B034/ C404/ D407/ 03	கவரகிரிய முனிஹின்கந்த தெருவின் முதல் ஒழுங்கை	160070.308/ 144121.318	160074.095/ 144115.104	159968.153/ 144113.02	159970.943/ 144111.919	150.67	3.0	2.5
292	SG/APS/ B034/ C404/ D407/ 04	கவரகிரிய முனிஹின்கந்த தெருவின் இரண்டாம் ஒழுங்கை	159794.826/ 144264.634	159797.389/ 144263.063	159768.364/ 144244.475	159770.02/ 144241.973	36.26	3.0	2.5
293	SG/APS/ B034/ C404/ D407/ 05	கவரகிரிய முனிஹின்கந்த தெருவின் மூன்றாம் ஒழுங்கை	159666.649/ 144453.8	159663.63/ 144455.816	159807.424/ 144467.393	159805.364/ 144469.573	164.01	3.0	2.5
294	SG/APS/ B034/ C404/ D407/ 06	கவரகிரிய முனிஹின்கந்த தெருவின் நான்காம் ஒழுங்கை	159448.12/ 144509.898	159444.09/ 144510.486	159608.707/ 144592.149	159610.995/ 144595.43	316.5	4.0	3.0
295	SG/APS/ B034/ C404/ D407/ 06/ 01	கவரகிரிய முனிஹின்கந்த தெருவின் நான்காம் ஒழுங்கையின் முதல் கிளைப்பாறை	159546.329/ 144610.2	159541.403/ 144611.997	159544.549/ 144642.438	159540.597/ 144643.056	35.18	4.0	3.0
296	SG/APS/ B034/ C404/ D407/ 07	கொலம்பேவ முனிஹின்கந்த இஹலகந்த தெரு	158971.526/ 144597.328	158969.03/ 144594.416	158120.112/ 145533.83	158116.754/ 145532.053	1357.05	3.8	3.0

தொ. இல.	தெருவின் குறியீடு	தெருவின் பெயர்	ஆரம்ப தொகுதி இலக்கங்கள் (கந்தவல இலங்கை)		இறுதித் தொகுதி இலக்கங்கள் (கந்தவல இலங்கை)		பாறை பொது வான நிலம் (மீற்றர்)	பாறை பொது வான நிலம் (மீற்றர்)	அபி விருத்தி அகலம் (மீற்றர்)
			இடம்	வலம்	இடம்	வலம்			
297	SG/ APS/ B034/ C404/ D407/ 07/ 01	கொலம்பேவ முனிவரின் கந்த இலககந்த தெருவின் முதல் ஒழுங்கை	158847.003/ 144733.997	158845.258/ 144738.239	159039.194/ 144981.19	159036.634/ 144983.272	428.42	3.3	3.0
298	SG/ APS/ B034/ C404/ D407/ 07/ 02	கொலம்பேவ முனிவரின் கந்த தொடம்கெவத்த தெரு	158696.391/ 144884.86	158699.492/ 144883.193	158634.513/ 144675.817	158636.259/ 144678.85	242.44	3.5	2.8
299	SG/ APS/ B034/ C404/ D407/ 07/ 03	கொலம்பேவ முனிவரின் கந்த ஐந்தாம் ஒழுங்கை	158542.604/ 145028.014	158538.637/ 145030.686	158714.365/ 145131.924	158714.169/ 145134.917	392.11	3.0	2.5
300	SG/ APS/ B034/ C404/ D407/ 07/ 03/ 01	கொலம்பேவ முனிவரின் கந்த ஐந்தாம் ஒழுங்கையின் முதல் கிளைப்பாறை	158590.991/ 145201.086	158587.689/ 145201.461	158695.52/ 145353.7	158696.379/ 145356.574	601.07	3.0	2.5
301	SG/ APS/ B034/ C404/ D407/ 08	கொலம்பேவ முனிவரின் கந்த ஐந்தாம் ஒழுங்கையின் ஆறாம் கிளைத் தெரு	158866.522/ 144388.389	158865.883/ 144385.255	158610.211/ 144338.245	158608.168/ 144336.049	291.71	3.0	2.5
302	SG/ APS/ B034/ C404/ C401/ 01	லந்தெ மெதேறென தெரு	163569.417/ 141308.403	163565.619/ 141309.094	163332.674/ 141668.101	163331.132/ 141664.958	469.6	3.5	2.5
303	SG/ APS/ B034/ C404/ C401/ 02	தும்பா மானான கலுவலர் ஹென தெரு	163944.518/ 141303.777	163948.493/ 141304.248	166245.219/ 139702.94	166244.348/ 139706.936	3549.34	4.0	3.5
304	SG/ APS/ B034/ C404/ C401/ 02/ 01	மஹவலவத்த கீழ்ப்பகுதி முதல் தெரு	166002.781/ 139632.525	166010.627/ 139627.027	164611.691/ 139486.328	164611.307/ 139482.347	1750.26	4.0	2.5

தொ. இல.	தெருவின் குறியீடு	தெருவின் பெயர்	ஆரம்ப தொகுதி இலக்கங்கள் (கந்தவல இலங்கை)		இறுதித் தொகுதி இலக்கங்கள் (கந்தவல இலங்கை)		பாதை பொது வான அகலம் (மீற்றர்)	பாதை பொது வான அகலம் (மீற்றர்)	அபி விருத்தி அகலம் (மீற்றர்)
			இடம்	வலம்	இடம்	வலம்			
305	SG/APS/ B034/ C404/ C401/ 02/ 01/ 01	மஹவலவத்த மேற்கு முதல் தெரு	165888.461/ 139579.195	165892.671/ 139580.48	165866.895/ 139267.512	165870.825/ 139266.768	4.0	4.0	3.0
306	SG/APS/ B034/ C404/ C401/ 02/ 01/ 02	மஹவலவத்த கீழ்ப்பகுதி இரண்டாம் தெரு	165627.987/ 139570.743	165623.85/ 139571.777	165642.93/ 139611.545	165640.391/ 139614.636	4.0	4.0	3.0
307	SG/APS/ B034/ C404/ C401/ 02/ 01/ 03	மஹவலவத்த மேற்கு இரண்டாம் தெரு	165489.395/ 139597.805	165494.258/ 139595.241	165390.308/ 139350.989	165393.146/ 139353.809	4.0	4.0	2.5
308	SG/APS/ B034/ C404/ C401/ 02/ 01/ 04	மஹவலவத்த கீழ்ப்பகுதி மூன்றாம் தெரு	165321.014/ 139668.669	165316.721/ 139668.115	165302.971/ 139736.613	165299.871/ 139734.989	3.5	3.5	2.5
309	SG/APS/ B034/ C404/ C401/ 02/ 01/ 05	சோதுருகந்த தெரு	164924.12/ 139470.482	164918.59/ 139471.973	164709.911/ 139695.183	164708.337/ 139691.506	4.0	4.0	2.5
310	SG/APS/ B034/ C404/ C401/ 02/ 02	தும்பர 02 ஆம் இலக்கத் தெரு	166065.85/ 139574.914	166069.315/ 139571.639	167182.273/ 138722.521	167178.712/ 138720.7	4.0	4.0	2.5
311	SG/APS/ B034/ C404/ C401/ 02/ 02/ 01	தும்பர 02 ஆம் இலக்கத் தெருவின் முதல் ஒழுங்கை	166130.695/ 139486.064	166134.467/ 139484.669	166278.353/ 139166.614	166282.224/ 139165.607	4.0	4.0	2.5
312	SG/APS/ B034/ C404/ C401/ 02/ 02/ 01/ 01	தும்பர 02 ஆம் இலக்கத் தெருவின் முதல் ஒழுங்கையின் முதல் கிளைப்பாதை	166146.247/ 139397.065	166152.835/ 139391.805	166076.601/ 139392.33	166075.03/ 139389.773	3.0	3.0	2.5

தொ. இல.	தெருவின் குறியீடு	தெருவின் பெயர்	ஆரம்ப தொகுதி இலக்கங்கள் (கந்தவல இலங்கை)		இறுதித் தொகுதி இலக்கங்கள் (கந்தவல இலங்கை)		பாறை பொது வான நிலம் (மீற்றர்)	பாறை பொது வான அகலம் (மீற்றர்)	அபி விருத்தி அகலம் (மீற்றர்)
			இடம்	வலம்	இடம்	வலம்			
313	SG/ APS/ B034/ C404/ C401/ 03	தும்பர மானான குட்டிகந்த தெரு	164164.67/ 141345.967	164158.941/ 141346.65	165891.23/ 142114.353	165896.228/ 142114.522	5413.49	5.0	2.5
314	SG/ APS/ B034/ C404/ C401/ 03/ 01	01 ஆம் இலக்க தும்பர மானான தெரு	164536.479/ 141436.909	164537.5/ 141440.87	167409.194/ 139926.99	167413.289/ 139928.864	3909.45	4.0	2.5
315	SG/ APS/ B034/ C404/ C401/ 03/ 02	தும்பர மானான பத்தல்மண்டிய தெரு	164380.898/ 141542.213	164377.625/ 141544.513	164052.052/ 142374.41	164051.034/ 142370.542	1216.5	4.0	2.6
316	SG/ APS/ B034/ C404/ C401/ 03/ 02/ 01	தும்பர மானான பத்தல்மண்டிய தெருவின் முதல் ஒழுங்கை	164459.644/ 141680.811	164456.362/ 141678.194	164138.131/ 141911.672	164137.558/ 141907.714	427.07	4.0	3.0
317	SG/ APS/ B034/ C404/ C401/ 03/ 02/ 02	தும்பர மானான பத்தல்மண்டிய தெருவின் இரண்டாம் ஒழுங்கை	164531.977/ 141828.718	164529.88/ 141831.622	164643.566/ 142030.531	164640.092/ 142030.108	257.64	3.5	2.5
318	SG/ APS/ B034/ C404/ C401/ 03/ 02/ 02/ 01	தும்பர மானான மியன்கல் குருந்த தெரு	164636.291/ 141954.722	164634.939/ 141959.151	165198.71/ 141807.634	165202.07/ 141804.641	631.81	4.5	2.5
319	SG/ APS/ B034/ C404/ C401/ 03/ 02/ 03	தும்பர மானான பத்தல்மண்டிய தெருவின் மூன்றாம் ஒழுங்கை	164258.957/ 142003.341	164262.152/ 141997.765	164100.798/ 142116.06	164099.281/ 142112.905	209.33	3.5	2.5
320	SG/ APS/ B034/ C404/ C401/ 03/ 03	தும்பர மானான குட்டிகந்த தெருவின் முதல் ஒழுங்கை	163635.671/ 142357.046	163633.06/ 142355.555	163354.38/ 142662.842	163352.065/ 142660.933	437.79	3.0	2.5

42A

IV (ஈ) கைபெ - ஸ்ரீ லக்ஷ்மீ பூசாநாத் சிவசபை அகலம் - 2026.01.01

பகுதி IV (ஆ) - இலங்கைச் சனநாயக சோசலிசக் குடியரசு வர்த்தமானப் பத்திரிகை - அதி விசேஷமானது - 2026.01.01

தொ. இல.	தெருவின் குறியீடு	தெருவின் பெயர்	ஆரம்ப தொகுதி இலக்கங்கள் (கந்தவல இலங்கை)		இறுதித் தொகுதி இலக்கங்கள் (கந்தவல இலங்கை)		பாதை பொது வான அகலம் (மீற்றர்)	பாதை பொது வான அகலம் (மீற்றர்)	அபி விருத்தி அகலம் (மீற்றர்)
			இடம்	வலம்	இடம்	வலம்			
321	SG/APS/ B034/ C404/ C401/ 03/ 04	தும்பர மானாள் 08 எக்கர் தெரு	163841.381/ 142762.389	163843.517/ 142765.997	164050.29/ 142644.156	164052.236/ 142640.66	284.95	4.0	2.6
322	SG/APS/ B034/ C404/ C401/ 03/ 05	தும்பர மானாள் குட்டிகந்த தெருவின் இரண்டாம் ஒழுங்கை	164428.871/ 142945.801	164432.902/ 142942.32	164393.2/ 142868.601	164393.885/ 142864.66	122.87	4.0	3.0
323	SG/APS/ B034/ C404/ C401/ 04	இலக்கம் 82 கோயில் அருகேயுள்ள பாதை	166942.524/ 139483.98	166935.276/ 139486.901	167628.782/ 139477.376	167628.157/ 139480.819	733.48	3.5	2.5
324	SG/APS/ B034/ C404/ C401/ 05	தும்பர 82 ஆம் இலக்க ஒற்றையடிப்பாதை	167105.569/ 139423.374	167107.583/ 139422.322	167227.378/ 138954.551	167229.145/ 138955.489	777.67	2.0	1.5
325	SG/APS/ B034/ C404/ C401/ 06	தும்பர 01 ஆம் இலக்கப் பாதை	168182.573/ 138870.069	168182.06/ 138874.932	167809.426/ 140441.934	167805.474/ 140442.553	2313.73	4.0	3.0
326	SG/APS/ B034/ C404/ C401/ 07	தும்பர மெதிகேல்ல மேல் தெரு	168219.125/ 138592.16	168214.867/ 138602.546	168972.466/ 138633.193	168973.006/ 138637.156	1081.8	4.0	2.5
327	SG/APS/ B034/ C404/ C401/ 08	மிணிபுர தும்பர தெரு	168635.217/ 138228.821	168631.853/ 138226.142	168544.386/ 138262.959	168540.747/ 138261.297	115.54	4.0	3.0
328	SG/APS/ B034/ C404/ C401/ 09	மிணிபுர தும்பர எட்டஹரலியகோட தெரு	168751.409/ 138073.939	168755.543/ 138073.175	168033.794/ 138501.759	168029.868/ 138502.53	1095.3	4.0	2.6

தொ. இல.	தெருவின் குறியீடு	தெருவின் பெயர்	ஆரம்ப தொகுதி இலக்கங்கள் (கந்தவல இலங்கை)		இறுதித் தொகுதி இலக்கங்கள் (கந்தவல இலங்கை)		பாறை பொது வான நீளம் (மீற்றர்)	பாறை பொது வான அகலம் (மீற்றர்)	அபி விருத்தி அகலம் (மீற்றர்)
			இடம்	வலம்	இடம்	வலம்			
329	SG/ APS/ B034/ C404/ C401/ 10	பெணிகலவத்த ஆற்றுத்துறைத் தெரு	168799.218/ 137902.52	168802.731/ 137898.96	170067.609/ 137559.462	170064.276/ 137563.216	4084.85	5.0	2.6
330	SG/ APS/ B034/ C404/ C401/ 10/ 01	தும்பர கலுவல தெரு	168157.401/ 137774.094	168157.087/ 137769.89	167997.597/ 138114.812	167995.529/ 138117.635	472.76	3.5	2.5
331	SG/ APS/ B034/ C404/ C401/ 10/ 02	பெணிகலவத்த ஆற்றுத்துறைத் தெருவின் முதல் ஒழுங்கை	168309.105/ 137506.554	168316.913/ 137504.135	168229.945/ 137508.79	168226.846/ 137506.262	98.39	4.0	3.0
332	SG/ APS/ B034/ C404/ C401/ 10/ 03	பெணிகலவத்த ஹல்வத்தூர தெரு	168712.289/ 137288.585	168716.23/ 137284.514	168665.296/ 137188.45	168669.989/ 137186.726	115.29	5.0	2.6
333	SG/ APS/ B034/ C404/ C401/ 10/ 04	பெணிகலவத்த ஆற்றுத்துறைத் தெருவின் இரண்டாம் ஒழுங்கை	168947.665/ 137212.914	168953.147/ 137210.257	168966.707/ 137126.2	168969.474/ 137128.342	101.26	3.5	2.0
334	SG/ APS/ B034/ C404/ C401/ 10/ 05	பெணிகலவத்த ஆற்றுத்துறைத் தெருவின் மூன்றாம் ஒழுங்கை	169420.173/ 137141.16	169423.788/ 137141.825	169384.294/ 136898.167	169387.592/ 136899.342	257.57	3.5	2.5
335	SG/ APS/ B034/ C404/ C401/ 10/ 06	பெணிகலவத்த ஆற்றுத்துறைத் தெருவின் நான்காம் ஒழுங்கை	169946.902/ 137056.331	169951.315/ 137055.014	169858.152/ 136653.153	169858.993/ 136649.243	651.13	4.0	2.1
336	SG/ APS/ B034/ C404/ C401/ 10/ 07	பெணிகலவத்த ஆற்றுத்துறைத் தெருவின் ஐந்தாம் ஒழுங்கை	169954.559/ 137054.354	169959.449/ 137054.23	170064.331/ 136947.26	170068.922/ 136946.957	176.83	4.6	4.0

தொ. இல.	தெருவின் குறியீடு	தெருவின் பெயர்	ஆரம்ப தொகுதி இலக்கங்கள் (கந்தவல இலங்கை)		இறுதித் தொகுதி இலக்கங்கள் (கந்தவல இலங்கை)		பாறை பொது வான அகலம் (மீற்றர்)	பாறை பொது வான அகலம் (மீற்றர்)	அபி விருத்தி அகலம் (மீற்றர்)
			இடம்	வலம்	இடம்	வலம்			
337	SG/APS/ B034/ C404/ C401/ 11	தொம்பையாவத்த ஆற்றுத்துறைத் தெரு	169590.917/ 138087.129	169585.055/ 138097.712	170081.326/ 137540.973	170084.233/ 137543.72	988.19	4.0	2.5
338	SG/APS/ B034/ C404/ C401/ 12	மெதப்பொல 01 ஆம் இலக்கப் பாறை	169568.796/ 138653.691	169568.472/ 138644.097	167450.006/ 139959.141	167446.501/ 139953.649	2699.67	3.5	2.5
339	SG/APS/ B034/ C404/ C401/ 13	பஹல்பொல முதல் தெரு	169603.301/ 138783.925	169616.912/ 138787.77	169853.565/ 138550.38	169855.909/ 138554.916	366.21	5.0	2.5
340	SG/APS/ B034/ C404/ C401/ 14	பஹல்பொல இரண்டாம் தெரு	169959.605/ 138553.252	169964.691/ 138549.087	170148.286/ 138438.809	170149.175/ 138442.708	455.02	4.0	3.0
341	SG/APS/ B034/ C404/ C401/ 14/ 01	பஹல்பொல இரண்டாம் தெருவின் முதல் ஒழுங்கை	169880.599/ 138506.303	169884.09/ 138506.695	170065.251/ 138101.546	170068.631/ 138102.455	515.72	3.5	2.5
342	SG/APS/ B034/ C404/ C401/ 14/ 02	பஹல்பொல இரண்டாம் தெருவின் இரண்டாம் ஒழுங்கை	170042.718/ 138459.316	170045.674/ 138458.35	170006.107/ 138388.362	170008.808/ 138386.793	87.99	3.0	2.0
343	SG/APS/ B034/ C404/ C401/ 14/ 03	பஹல்பொல இரண்டாம் தெருவின் மூன்றாம் ஒழுங்கை	170120.979/ 138439.662	170123.481/ 138439.708	170025.403/ 138374.488	170027.377/ 138372.639	135.11	2.5	2.5
344	SG/APS/ B034/ C404/ C401/ 15	பஹல்பொல மூன்றாம் தெரு	170094.887/ 138614.153	170098.645/ 138615.552	170189.197/ 138604.204	170185.914/ 138606.488	120.09	4.0	2.5

தொ. இல.	தெருவின் குறியீடு	தெருவின் பெயர்	ஆரம்ப தொகுதி இலக்கங்கள் (கந்தவல இலங்கை)		இறுதித் தொகுதி இலக்கங்கள் (கந்தவல இலங்கை)		பாறை பொது வான நிலம் (மீற்றர்)	பாறை பொது வான அகலம் (மீற்றர்)	அபி விருத்தி அகலம் (மீற்றர்)
			இடம்	வலம்	இடம்	வலம்			
345	SG/ APS/ B034/ C404/ C401/ 15/ 01	பஹலபொல முன்றாம் தெருவின் முதல் ஒழுங்கை	170108.994/ 138589.081	170111.809/ 138586.657	170121.508/ 138443.672	170124.792/ 138443.741	163.95	3.0	2.5
346	SG/ APS/ B034/ C402/ 01	அயகம எலபாத்த தெருவின் முதல் ஒழுங்கை	159461.777/ 149379.181	159458.973/ 149381.326	159387.298/ 149574.851	159385.347/ 149571.943	256.14	3.5	3.0
347	SG/ APS/ B034/ C402/ 01/ 01	அயகம எலபாத்த தெருவின் முதல் ஒழுங்கையின் முதல் கிளைப் பாறை	159423.585/ 149522.478	159424.399/ 149525.883	159502.077/ 149478.071	159503.732/ 149481.156	93.1	3.5	3.0
348	SG/ APS/ B034/ C402/ 02	சரத்புர நடுத் தெரு	159447.649/ 149388.194	159450.001/ 149384.943	159232.965/ 149320.121	159236.74/ 149318.507	300.32	4.0	3.0
349	SG/ APS/ B034/ C402/ 02/ 01	சரத்புர நடுத் தெருவின் முதல் ஒழுங்கை	159382.923/ 149306.953	159382.727/ 149304.453	159306.148/ 149352.255	159304.278/ 149350.595	93.78	2.5	1.0
350	SG/ APS/ B034/ C402/ 02/ 02	சரத்புர நடுத் தெருவின் இரண்டாம் ஒழுங்கை	159255.574/ 149335.976	159252.454/ 149334.811	159277.353/ 149390.737	159276.866/ 149393.697	66.48	3.0	3.0
351	SG/ APS/ B034/ C402/ 03	சரத்புர முதல் ஒழுங்கை	159381.676/ 149465.264	159383.42/ 149462.67	159240.917/ 149429.631	159241.003/ 149426.547	155.78	3.0	3.0
352	SG/ APS/ B034/ C402/ 04	அயகம எலபாத்த தெருவின் இரண்டாம் ஒழுங்கை	159389.948/ 149582.055	159387.143/ 149580.654	159326.662/ 149723.997	159323.688/ 149723.605	197.56	3.0	3.0

தொ. இல.	தெருவின் குறியீடு	தெருவின் பெயர்	ஆரம்ப தொகுதி இலக்கங்கள் (கந்தவல இலங்கை)		இறுதித் தொகுதி இலக்கங்கள் (கந்தவல இலங்கை)		பாதை பொது வான அகலம் (மீற்றர்)	அபி விருத்தி அகலம் (மீற்றர்)
			இடம்	வலம்	இடம்	வலம்		
353	SG/APS/ B034/ C402/ 05	அயகம எலபாத்த தெருவின் மூன்றாம் ஒழுங்கை	159537.463/ 149681.071	159537.114/ 149684.57	159592.073/ 149643.185	159591.783/ 149646.672	3.5	3.5
354	SG/APS/ B034/ C402/ 06	அயகம எலபாத்த தெருவின் நான்காம் ஒழுங்கை	159510.747/ 149768.346	159511.485/ 149764.748	159257.203/ 149882.453	159256.039/ 149879.153	3.5	3.5
355	SG/APS/ B034/ C402/ 07	சமருகம் நடுத்த தெரு	159379.418/ 149957.766	159379.92/ 149954.302	159165.735/ 149699.736	159169.01/ 149701.016	3.5	3.0
356	SG/APS/ B034/ C402/ 08	அயகம எலபாத்த தெருவின் ஐந்தாம் ஒழுங்கை	159279.654/ 150104.126	159277.422/ 150106.134	159689.449/ 149943.843	159686.7/ 149945.045	3.0	3.0
357	SG/APS/ B034/ C402/ 09	அயகம எலபாத்த தெருவின் ஆறாம் ஒழுங்கை	159128.731/ 150373.43	159126.751/ 150370.511	158792.732/ 150542.001	158795.844/ 150540.399	3.5	3.0
358	SG/APS/ B034/ C402/ 10	அயகம எலபாத்த தெருவின் ஏழாம் ஒழுங்கை	159741.171/ 150667.187	159740.058/ 150670.378	160130.92/ 150920.892	160129.531/ 150923.551	3.0	3.0
359	SG/APS/ B034/ D401/ 01	உடுகல் கெந்தகல் தெரு	157287.745/ 150320.142	157291.64/ 150321.053	156313.654/ 146716.075	156316.312/ 146713.085	4.0	3.5
360	SG/APS/ B034/ D401/ 01/ 01	பயின்னில் தோட்டப் தோட்டத் தெரு	157208.055/ 150206.886	157209.151/ 150203.024	156709.13/ 150088.967	156713.044/ 150089.79	4.0	4.0

தொ. இல.	தெருவின் குறியீடு	தெருவின் பெயர்	ஆரம்ப தொகுதி இலக்கங்கள் (கந்தவல இலங்கை)		இறுதித் தொகுதி இலக்கங்கள் (கந்தவல இலங்கை)		பாதை பொது வான நளம் (மீற்றர்)	பாதை பொது வான அகலம் (மீற்றர்)	அபி விருத்தி அகலம் (மீற்றர்)
			இடம்	வலம்	இடம்	வலம்			
361	SG/ APS/ B034/ D401/ 01/ 02	பயின்ஹில் குடியேற்றத் தெரு	157320.013/ 149886.172	157317.269/ 149883.871	156982.264/ 149661.686	156985.239/ 149659.842	566.71	3.5	3.0
362	SG/ APS/ B034/ D401/ 01/ 02/ 01	பயின்ஹில் மேல் தெரு	157227.648/ 149894.143	157225.013/ 149892.709	157160.356/ 149888.568	157163.081/ 149887.312	95.31	3.0	3.0
363	SG/ APS/ B034/ D401/ 01/ 02/ 02	பயின்ஹில் குடியேற்றம் கெந்தகல தெரு	157133.609/ 149725.826	157137.132/ 149726.868	157065.731/ 149589.514	157069.925/ 149590.522	159.34	3.0	2.0
364	SG/ APS/ B034/ D401/ 01/ 02/ 03	பயின்ஹில் குடியேற்றம் கெந்தகல தெருவின் முதல் ஒழுங்கை	157030.221/ 149714.53	157027.327/ 149713.727	156910.603/ 149791.995	156908.828/ 149789.577	189.46	3.0	3.0
365	SG/ APS/ B034/ D401/ 01/ 03	உடுகல பிட்டகந்த கிராம சபை முதல் தெரு	157326.54/ 149849.629	157323.621/ 149852.496	157404.109/ 149821.606	157407.586/ 149823.594	114.46	4.0	3.0
366	SG/ APS/ B034/ D401/ 01/ 04	உடுகல பிட்டகந்த கிராம சபை இரண்டாம் தெரு	157324.255/ 149782.296	157324.224/ 149785.299	157456.781/ 149792.983	157456.728/ 149795.982	155.48	3.0	3.0
367	SG/ APS/ B034/ D401/ 01/ 05	புபுலஹேன தெரு	157310.794/ 149645.707	157312.533/ 149648.173	157543.494/ 149446.695	157542.715/ 149449.591	352.37	3.0	2.0
368	SG/ APS/ B034/ D401/ 01/ 06	உடுகல கெந்தகல கிராம சபைத் தெரு	157154.466/ 149534.557	157151.607/ 149533.449	156816.662/ 149478.874	156818.62/ 149481.149	472.18	3.0	2.0

தொ. இல.	தெருவின் குறியீடு	தெருவின் பெயர்	ஆரம்ப தொகுதி இலக்கங்கள் (கந்தவல இலங்கை)		இறுதித் தொகுதி இலக்கங்கள் (கந்தவல இலங்கை)		பாதை பொது வான அகலம் (மீற்றர்)	அபி விருத்தி அகலம் (மீற்றர்)
			இடம்	வலம்	இடம்	வலம்		
369	SG/APS/ B034/ D401/ 01/ 07	கனத்தா எல்வெல்லேன தெரு	156822.356/ 149378.184	156821.703/ 149375.114	156698.037/ 149406.824	156696.315/ 149404.368	3.0	3.0
370	SG/APS/ B034/ D401/ 01/ 08	உடுகல கெந்தகல் தெருவின் முதல் ஒழுங்கை	156811.451/ 149337.844	156811.69/ 149334.842	156763.994/ 149303.041	156765.413/ 149300.397	3.0	3.0
371	SG/APS/ B034/ D401/ 01/ 09	கெந்தகல் பழைய கிராம சபைத் தெரு	156684.691/ 148304.064	156681.118/ 148302.226	156549.574/ 148301.897	156552.931/ 148304.161	4.0	4.0
372	SG/APS/ B034/ D401/ 01/ 10	கெந்தகல் ஆரணியத் தெரு	156663.245/ 147217.589	156663.011/ 147221.128	156856.926/ 147066.015	156858.919/ 147068.892	3.5	3.0
373	SG/APS/ B034/ D401/ 01/ 11	கெந்தகல் ஹத்தலிஹ வத்த தெரு	156531.734/ 147168.814	156534.705/ 147170.276	156588.076/ 146855.55	156590.973/ 146856.33	3.0	2.5
374	SG/APS/ B034/ D401/ 01/ 12	கெந்தகல் மில்லேன ஒற்றையடிப்பாதை	156514.649/ 147164.072	156512.859/ 147162.653	156399.529/ 147315.415	156397.529/ 147315.453	2.0	1.0
375	SG/APS/ B034/ D401/ 01/ 13	கெந்தகல் மில்லேன தெரு	156465.693/ 147104.555	156464.318/ 147100.354	155868.854/ 147300.375	155871.845/ 147303.031	4.0	3.0
376	SG/APS/ B034/ D401/ 01/ 13/ 01	கெந்தகல் மில்லேன தெருவின் முதல் ஒழுங்கை	155798.488/ 147446.75	155800.358/ 147442.241	155757.427/ 147412.9	155760.911/ 147413.242	3.5	2.5

தொ. இல.	தெருவின் குறியீடு	தெருவின் பெயர்	ஆரம்ப தொகுதி இலக்கங்கள் (கந்தவல இலங்கை)		இறுதித் தொகுதி இலக்கங்கள் (கந்தவல இலங்கை)		பாதை பொது வான நீளம் (மீற்றர்)	பாதை பொது வான அகலம் (மீற்றர்)	அபி விருத்தி அகலம் (மீற்றர்)
			இடம்	வலம்	இடம்	வலம்			
377	SG/ APS/ B034/ D401/ 01/ 14	ஹட்கிரிதொல மின்சார நிலைய தெரு	156317.778/ 146714.349	156320.348/ 146716.86	157384.536/ 146089.61	157388.032/ 146089.765	1505.66	3.5	2.5
378	SG/ APS/ B034/ D401/ 02	உடுகல அங்குருவெல தெருவின் முதல் ஒழுங்கை	157148.367/ 150420.874	157150.959/ 150419.323	156956.706/ 150276.248	156955.504/ 150273.499	276.08	3.0	3.0
379	SG/ APS/ B034/ D401/ 02/ 01	ஸ்ரீ தர்மரக்சிதாராமய தெரு	157080.52/ 150372.702	157078.667/ 150369.666	157022.099/ 150382.247	157020.6/ 150379.648	61.74	3.0	3.0
380	SG/ APS/ B034/ D401/ 03	உடுகல அங்குருவெல தெருவின் இரண்டாம் ஒழுங்கை	156827.768/ 150588.171	156824.818/ 150587.482	156791.117/ 150679.513	156788.524/ 150678.006	102.04	3.0	3.0
381	SG/ APS/ B034/ D401/ 04	அங்குருவெல பயின்ஹில் தோட்டம் முதல் ஒழுங்கை	156693.755/ 150550.761	156696.529/ 150551.993	156751.097/ 150216.214	156753.191/ 150218.367	546.79	3.0	2.5
382	SG/ APS/ B034/ D401/ 05	உடுகல அங்குருவெல தெருவின் மூன்றாம் ஒழுங்கை	156584.485/ 150624.643	156582.288/ 150627.259	156643.239/ 150734.101	156640.736/ 150732.446	153.86	3.0	2.5
383	SG/ APS/ B034/ D401/ 06	ஹந்துன்கந்த பட்டேஹை தெரு	156040.438/ 150792.897	156036.998/ 150795.111	156122.938/ 150988.518	156122.743/ 150992.513	327.12	4.0	2.6
384	SG/ APS/ B034/ D401/ 06/ 01	ஹந்துன்கந்த பட்டேஹை தெருவின் முதல் ஒழுங்கை	156062.901/ 151020.222	156058.403/ 151020.36	156121.892/ 151137.242	156119.409/ 151140.995	157.53	4.5	2.0

50A

IV (ஈ) கைபெ - ஸ்ரீ லக்ஷ்மீ ப்ரதீகாபீகா க்ரதீகாபீகா - 2026.01.01

பகுதி IV (ஆ) - இலங்கைச் சனநாயக சோசலிசக் குடியரசு வர்த்தமானப் பத்திரிகை - அதி விசேஷமானது - 2026.01.01

தொ. இல.	தெருவின் குறியீடு	தெருவின் பெயர்	ஆரம்ப தொகுதி இலக்கங்கள் (கந்தவல இலங்கை)		இறுதித் தொகுதி இலக்கங்கள் (கந்தவல இலங்கை)		பாதை பொது வான அகலம் (மீற்றர்)	பாதை பொது வான அகலம் (மீற்றர்)	அபி விருத்தி அகலம் (மீற்றர்)
			இடம்	வலம்	இடம்	வலம்			
385	SG/APS/ B034/ D401/ 07	ஹந்துன்கந்த பாடசாலைத் தெரு	155993.968/ 150808.67	155990.983/ 150808.333	155932.163/ 150913.026	155929.876/ 150914.969	3.0	3.0	2.0
386	SG/APS/ B034/ D401/ 08	ஹந்துன்கந்த முதல் ஒழுங்கை	155941.04/ 150567.698	155942.719/ 150571.068	156052.536/ 150397.226	156055.058/ 150399.652	3.5	3.5	2.5
387	SG/APS/ B034/ D401/ 09	அங்குருவெல பயின்ஹில் தோட்டம் இரண்டாம் ஒழுங்கை	155416.689/ 150299.172	155423.355/ 150297.887	156700.848/ 150198.96	156696.86/ 150194.851	4.0	4.0	2.5
388	SG/APS/ B034/ D401/ 10	உடுகல அங்குருவெல தெருவின் நான்காம் ஒழுங்கை	155255.126/ 150278.066	155258.442/ 150279.193	155301.796/ 150099.024	155303.867/ 150101.844	3.5	3.5	3.0
389	SG/APS/ B034/ D401/ 11	அங்குருவெல தாங்கி ஒற்றையடிப்பாதை	154924.975/ 150380.579	154922.681/ 150383.016	154917.22/ 151066.195	154917.112/ 151069.193	3.0	3.0	2.0
390	SG/APS/ B034/ D401/ 12	பன்விலேஹை முதல் ஒழுங்கை	154663.695/ 150905.562	154663.531/ 150901.319	154547.724/ 151089.588	154544.204/ 151091.487	4.0	4.0	3.0
391	SG/APS/ B034/ D401/ 13	அங்குருவெல பன்விலேஹை தெரு	154671.092/ 150934.792	154668.105/ 150935.088	154379.255/ 151278.751	154379.522/ 151275.763	3.0	3.0	3.0
392	SG/APS/ B034/ D401/ 13/ 01	பன்விலேஹை இரண்டாம் ஒழுங்கை - ஒற்றையடிப்பாதை	154643.94/ 151182.473	154640.685/ 151184.567	154534.83/ 151309.855	154534.658/ 151306.859	3.0	3.0	1.0

தொ. இல.	தெருவின் குறியீடு	தெருவின் பெயர்	ஆரம்ப தொகுதி இலக்கங்கள் (கந்தவல இலங்கை)		இறுதித் தொகுதி இலக்கங்கள் (கந்தவல இலங்கை)		பாறை பொது வான நீளம் (மீற்றர்)	பாறை பொது வான அகலம் (மீற்றர்)	அபி விருத்தி அகலம் (மீற்றர்)
			இடம்	வலம்	இடம்	வலம்			
393	SG/ APS/ B034/ C403/ 01	வேகம்கந்த தெரு	153527.299/ 154057.44	153527.251/ 154061.441	154282.721/ 153664.727	154279.844/ 153667.505	989.79	4.0	4.0
394	SG/ APS/ B034/ C403/ 02	குக்குலுவா ரஜமஹா விஹாரை முதல் மாவத்த	153415.092/ 154520.334	153416.359/ 154526.083	154548.876/ 155593.224	154549.724/ 155596.62	2129.06	3.5	3.0
395	SG/ APS/ B034/ C403/ 02/ 01	கரவிலஹேன்யாய தெரு	153688.552/ 154709.874	153688.286/ 154714.284	153796.476/ 154135.909	153799.374/ 154136.687	788.25	3.0	2.5
396	SG/ APS/ B034/ C403/ 03	வெல்லவத்த நாவின்ன தெரு	153491.897/ 154877.567	153490.694/ 154874.125	153259.975/ 154932.132	153257.195/ 154930.006	306.89	3.5	3.0
397	SG/ APS/ B034/ C403/ 04	குக்குலுவா ரஜமஹா விஹாரை ஒற்றையடிப்பாதை	153515.858/ 154959.691	153515.612/ 154961.225	153738.21/ 155002.228	153738.768/ 155003.684	247.55	1.5	1.5
398	SG/ APS/ B034/ C403/ 05	நாவின்ன தோட்ட தேவாலயத் தெரு	153482.602/ 155076.016	153484.102/ 155072.29	153258.283/ 155086.651	153261.462/ 155085.185	312.38	3.5	3.5
399	SG/ APS/ B034/ C403/ 06	நாவின்ன தோட்டம் குரஹனத் தெரு	153329.396/ 155519.527	153332.445/ 155516.448	153150.443/ 155626.267	153150.56/ 155630.266	364.51	4.0	3.0
400	SG/ APS/ B034/ C403/ 06/ 01	நாவின்ன தோட்டம் மடித்த தெரு	153156.402/ 155509.905	153159.597/ 155508.082	152728.705/ 155356.83	152726.554/ 155354.461	1343.14	3.2	3.0

52A

IV (ஈ) கைபெ - ஸ்ரீ லக்ஷ்மீ ப்ரதீபாதி க்ஷத்ரபெ - 2026.01.01

பகுதி IV (ஆ) - இலங்கைச் சனநாயக சோசலிசக் குடியரசு வர்த்தமானப் பத்திரிகை - அதி விசேஷமானது - 2026.01.01

தொ- இல.	தெருவின் குறியீடு	தெருவின் பெயர்	ஆரம்ப தொகுதி இலக்கங்கள் (கந்தவல இலங்கை)		இறுதித் தொகுதி இலக்கங்கள் (கந்தவல இலங்கை)		பாதை பொது வான் நீளம் (மீற்றர்)	பாதை பொது வான் அகலம் (மீற்றர்)	அபி விருத்தி அகலம் (மீற்றர்)
			இடம்	வலம்	இடம்	வலம்			
401	SG/APS/ B034/ C403/ 07	பிம்புர கலவான தெரு	153417.591/ 155745.569	153416.569/ 155740.593	152709.9/ 156242.322	152708.631/ 156237.485	1060.64	5.0	4.0
402	SG/APS/ B034/ C403/ 07/ 01	தென்னேன தெரு	152870.605/ 156202.46	152865.714/ 156201.659	153234.208/ 156678.36	153231.423/ 156675.489	1137.57	4.0	3.0
403	SG/APS/ B034/ C403/ 08	குக்குலுவா ரஜமஹா விஹாரை இரண்டாம் மாவத்த	153463.565/ 156000.401	153462.728/ 156003.372	154024.251/ 155442.209	154026.865/ 155440.112	864.91	3.0	3.0
404	SG/APS/ B034/ C403/ 09	பிம்புர கரவிட்ட தெருவின் முதல் ஒழுங்கை	153460.226/ 156158.501	153460.447/ 156165.711	153510.578/ 156229.595	153508.374/ 156232.314	90.02	3.5	3.0
405	SG/APS/ B034/ C403/ 10	பிம்புர கரவிட்ட தெருவின் இரண்டாம் ஒழுங்கை	153459.349/ 156263.282	153460.227/ 156267.562	153532.008/ 156308.444	153530.977/ 156311.79	89.52	3.5	3.0
406	SG/APS/ B421/ C428/ 01	குக்குலெகம் ஜாத்துவங்கொட தெருவின் முதல் ஒழுங்கை	153463.408/ 150016.386	153462.085/ 150021.274	154167.955/ 149520.647	154171.478/ 149517.099	979.21	5.0	3.0
407	SG/APS/ B421/ C428/ 02	நிதன்கல பன்சலைத் தெரு	153121.918/ 149082.771	153121.754/ 149078.768	152640.684/ 149889.154	152636.832/ 149890.232	1216.06	4.0	2.5









62A

IV(ஈ) : கைஓ஑ - ஸ்ரீ லு஑ா ஸ்ர஑ா஑ா஑்஑ு஑ ஑லா஑லா஑ீ ஑஑ர஑஑ீ ஑஑ி லீ஑஑ ஑஑஑ ஑஑஑ - 2026.01.01

஑஑ு஑ி IV(஑) - இல஑஑஑஑஑ ஑஑஑஑஑஑ ஑ோ஑஑஑஑஑ ஑ு஑஑஑஑ வ஑்஑஑஑஑஑ ஑஑஑஑஑஑஑ - ஑஑஑ி வ஑஑஑஑஑஑஑஑ - 2026.01.01
















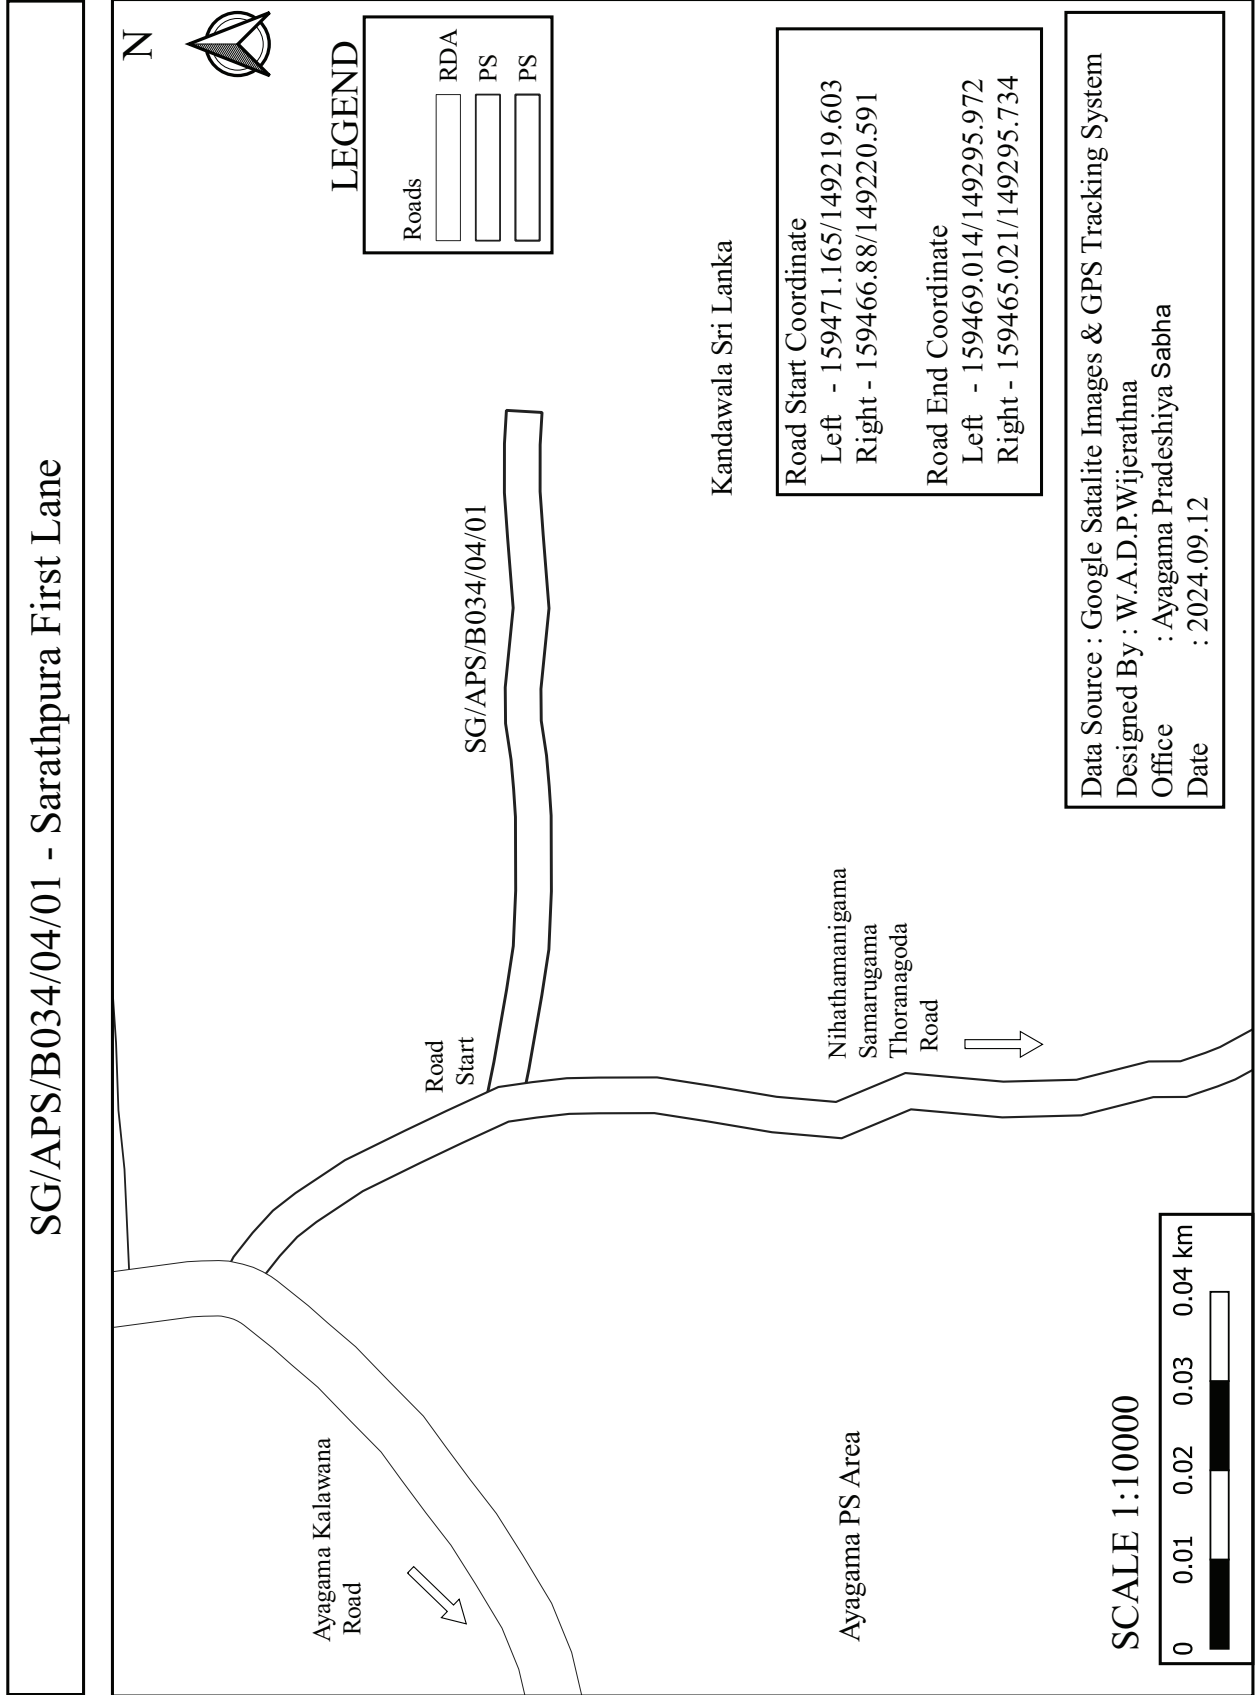

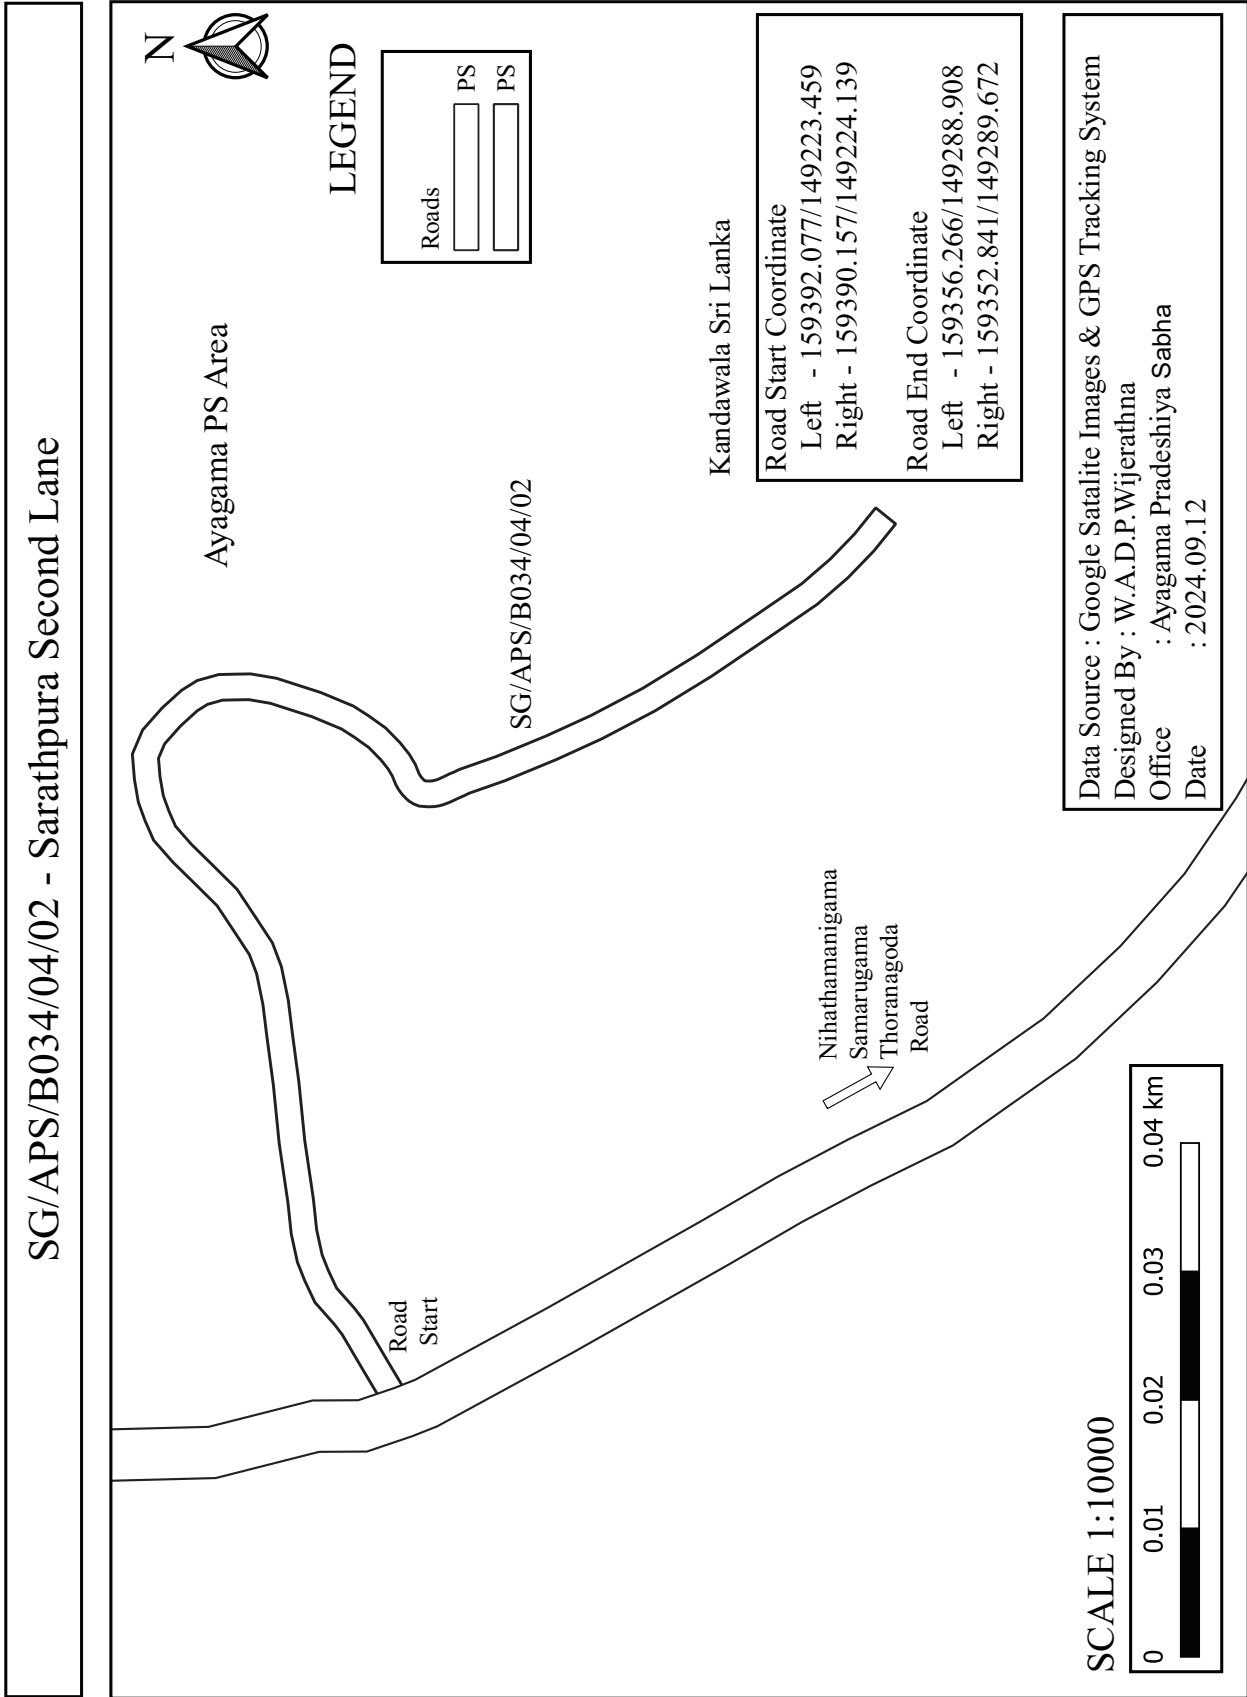


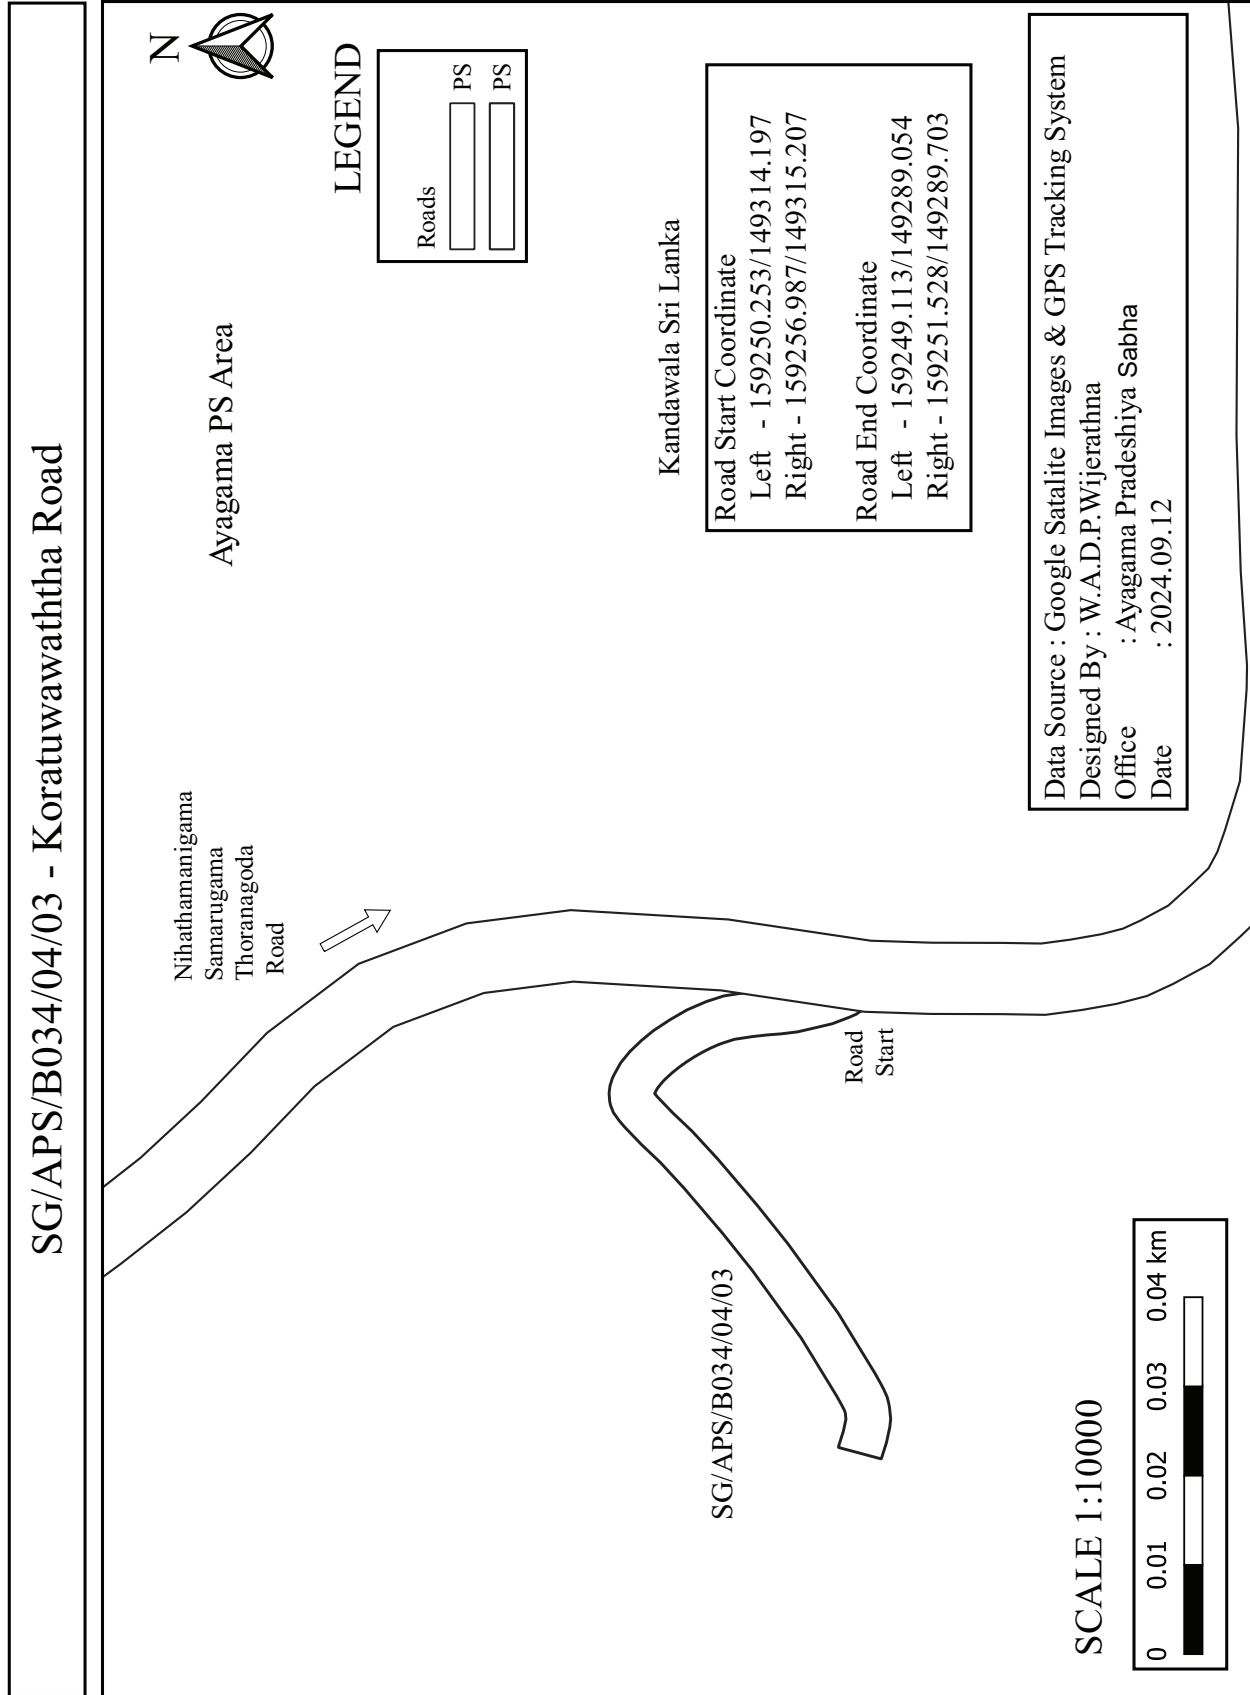

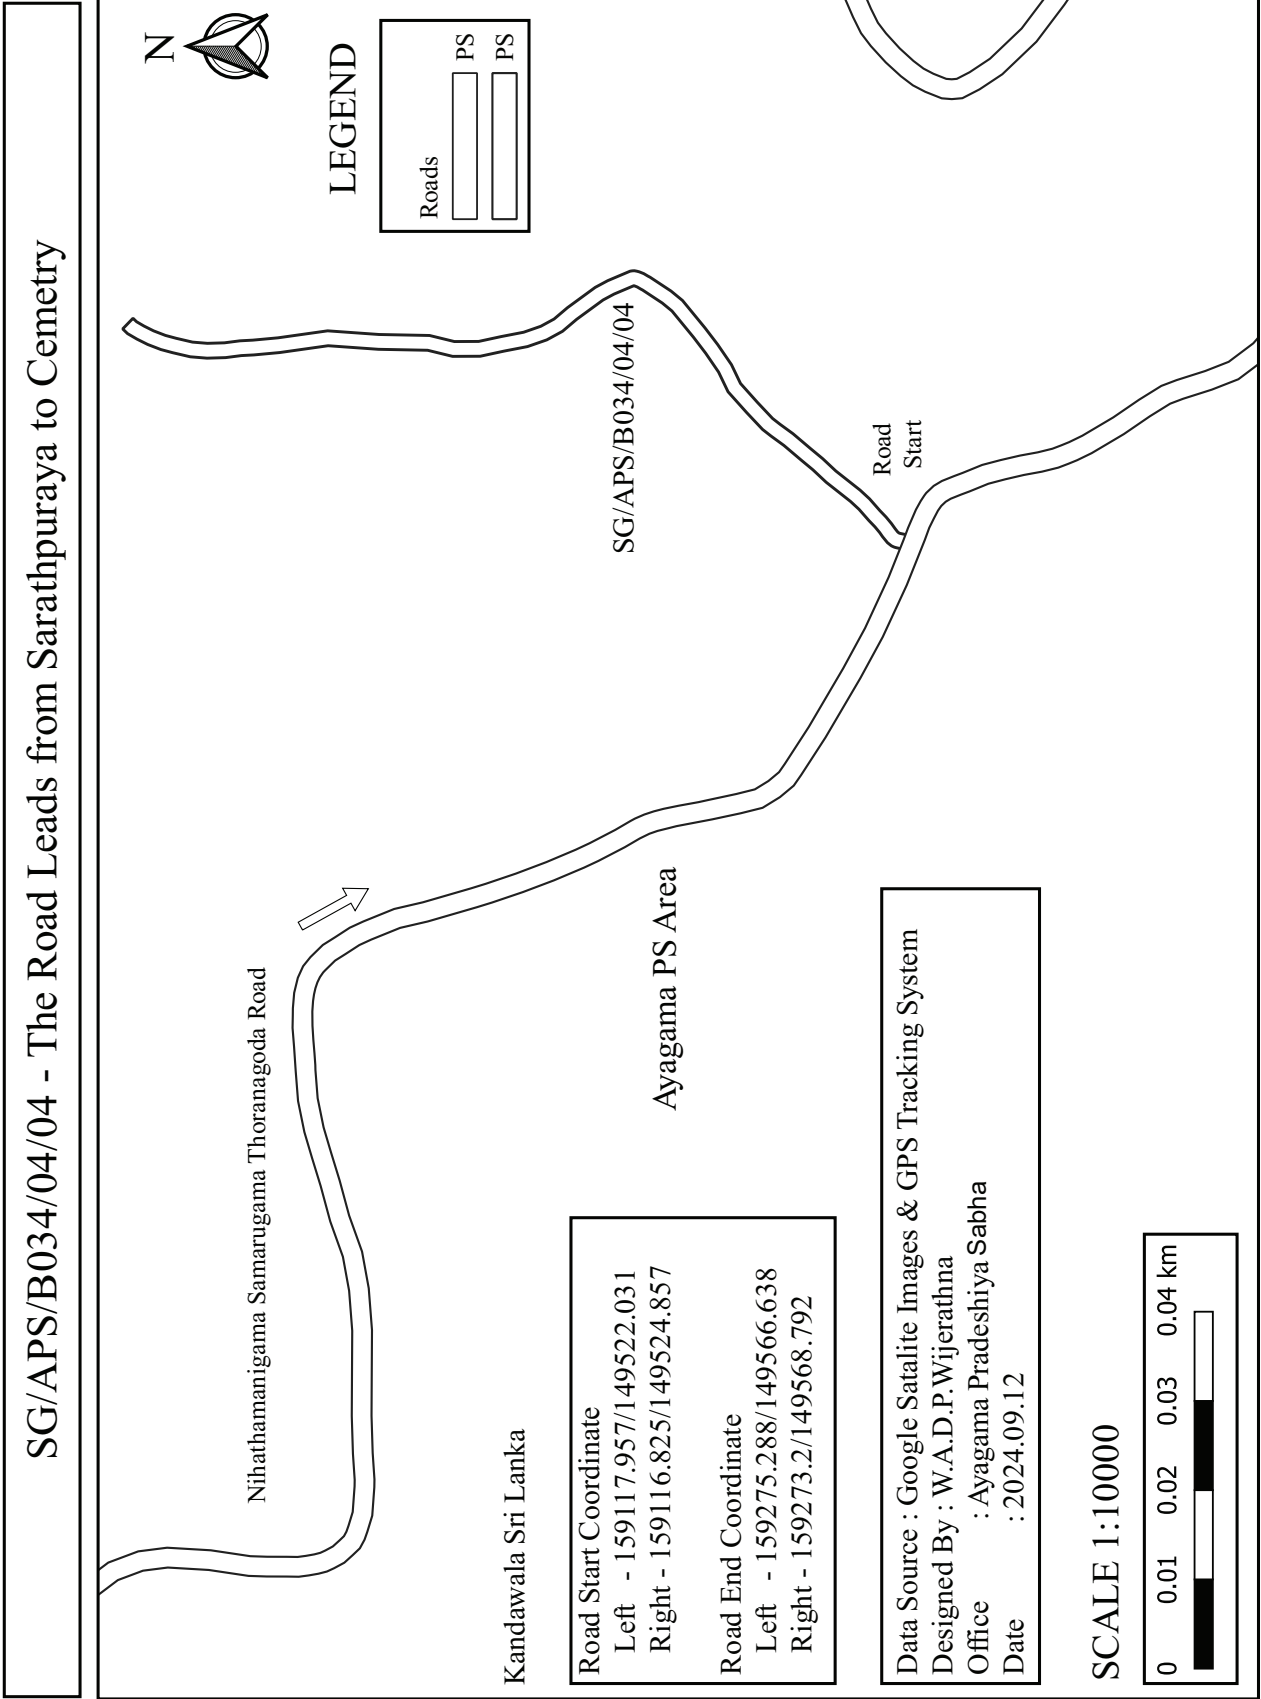


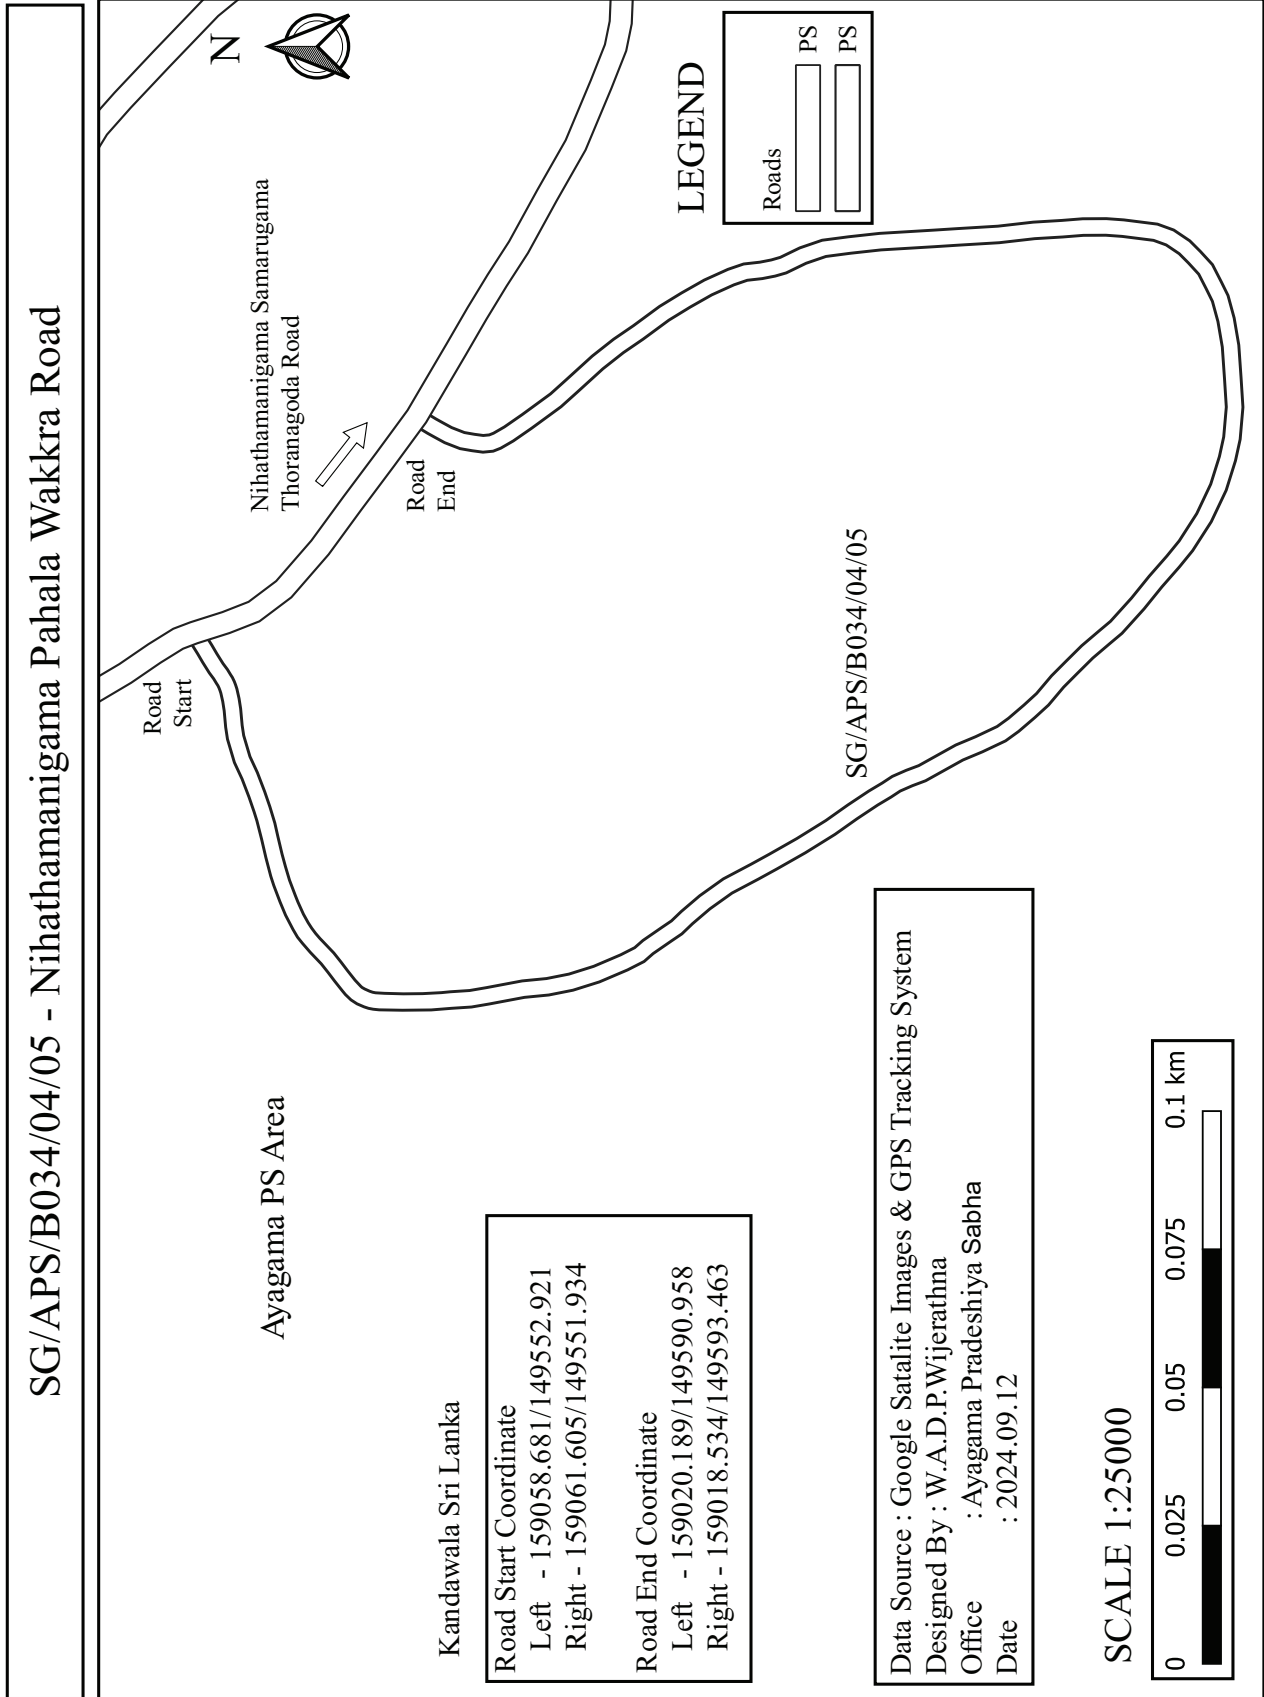



SG/APS/B034/04/06 - Nihathamanigama Beraliyana Road

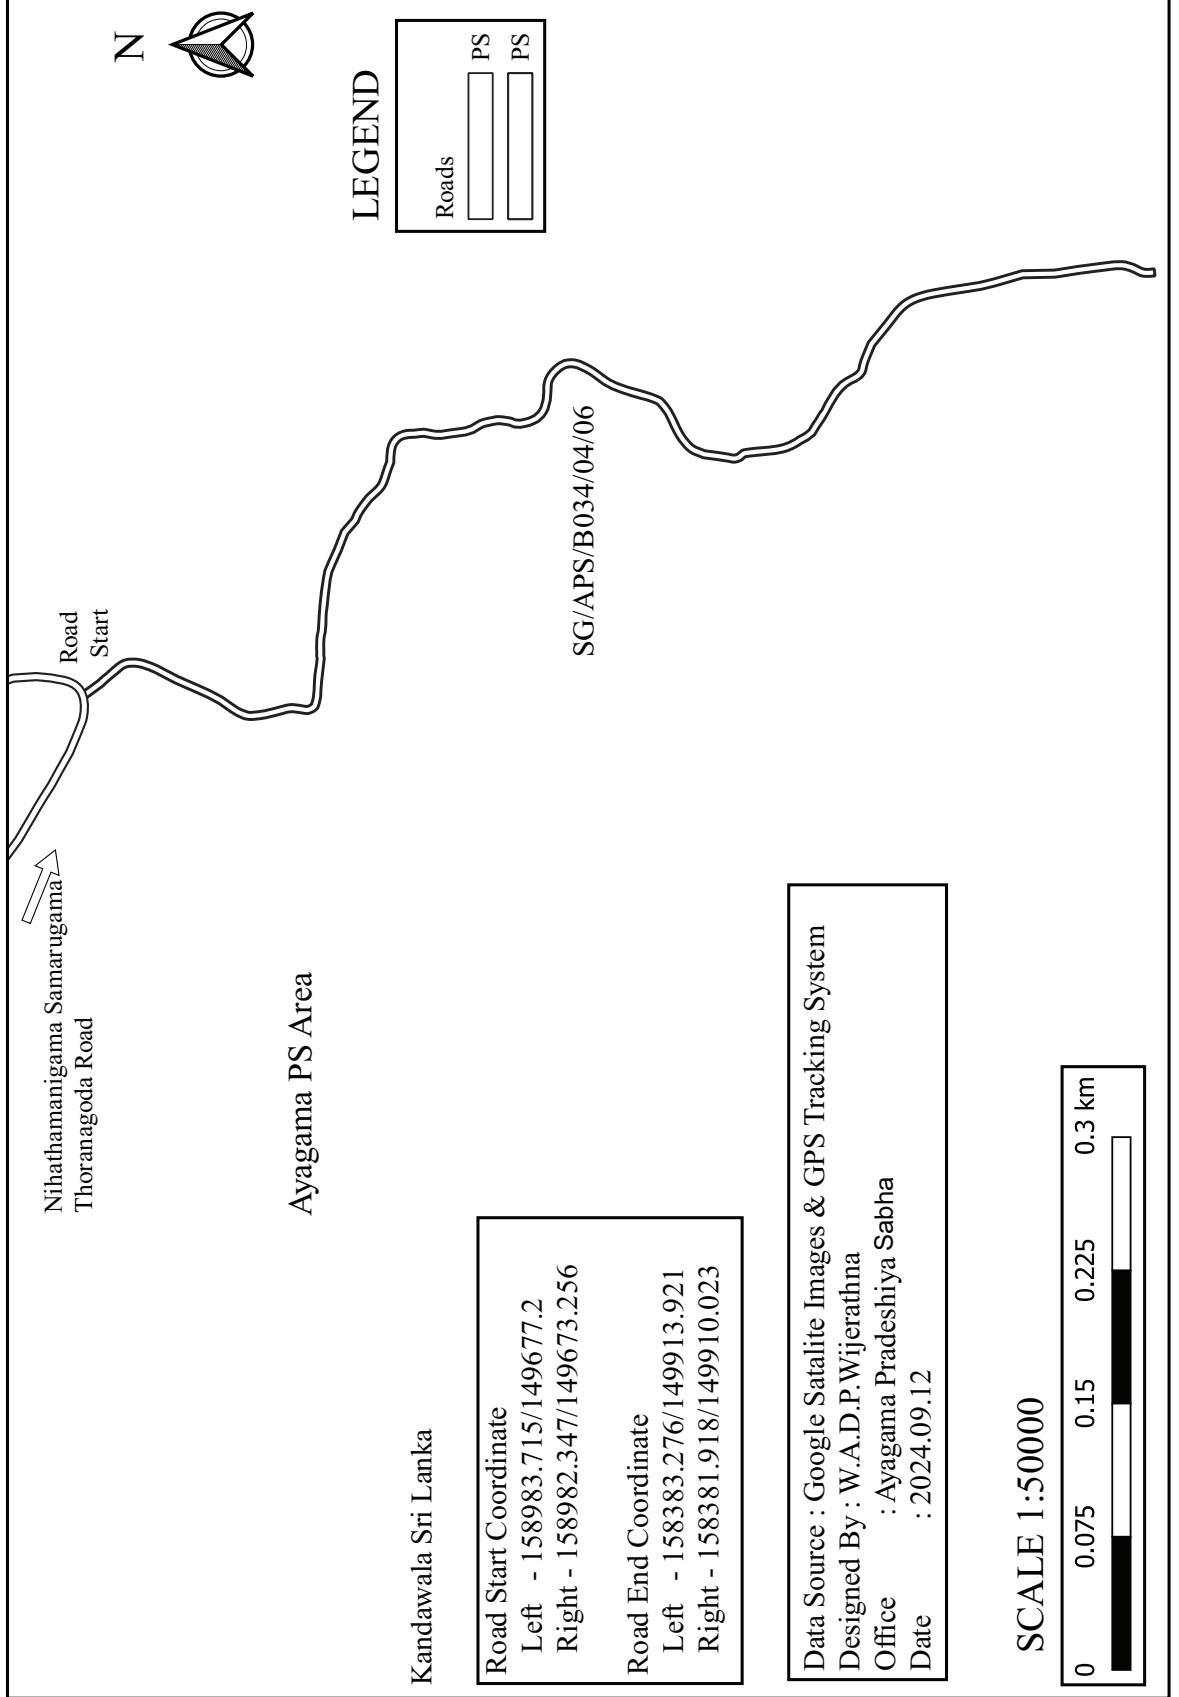



Kandawala Sri Lanka

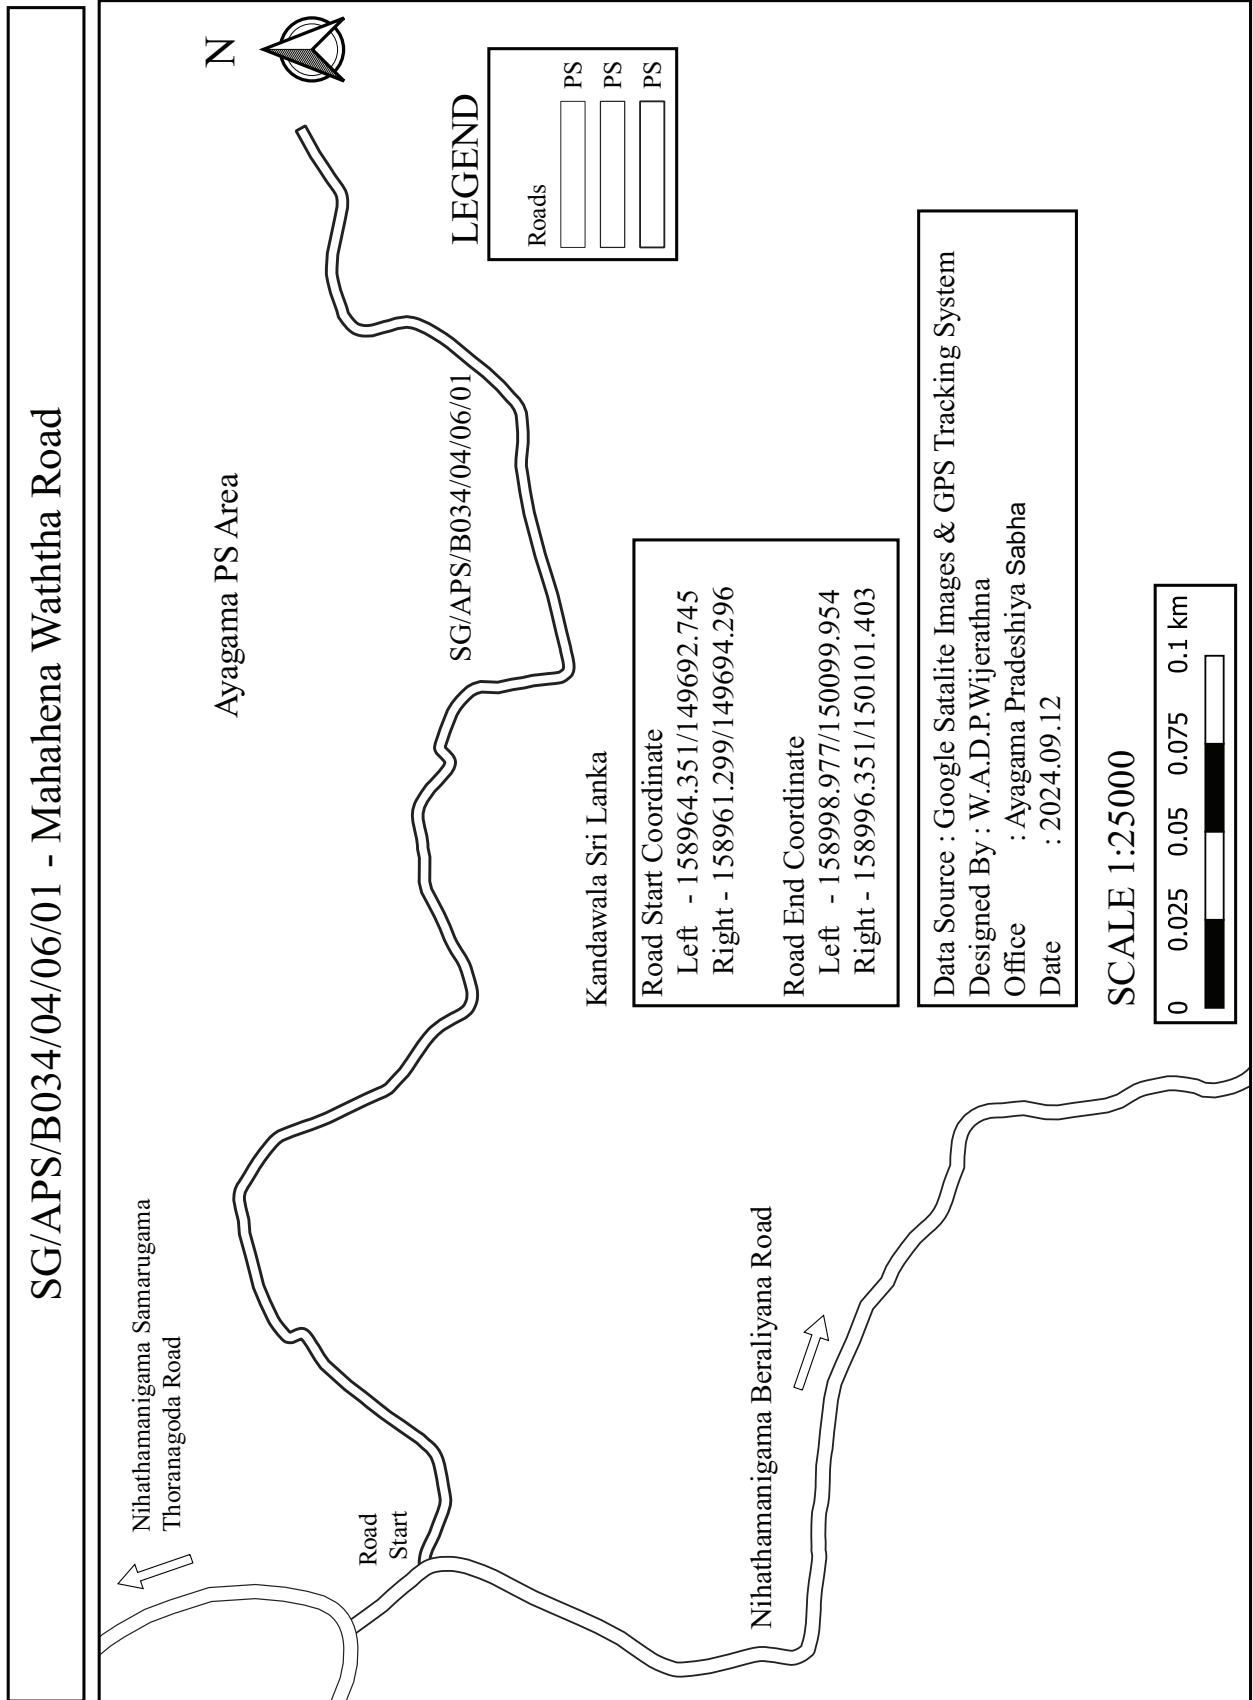


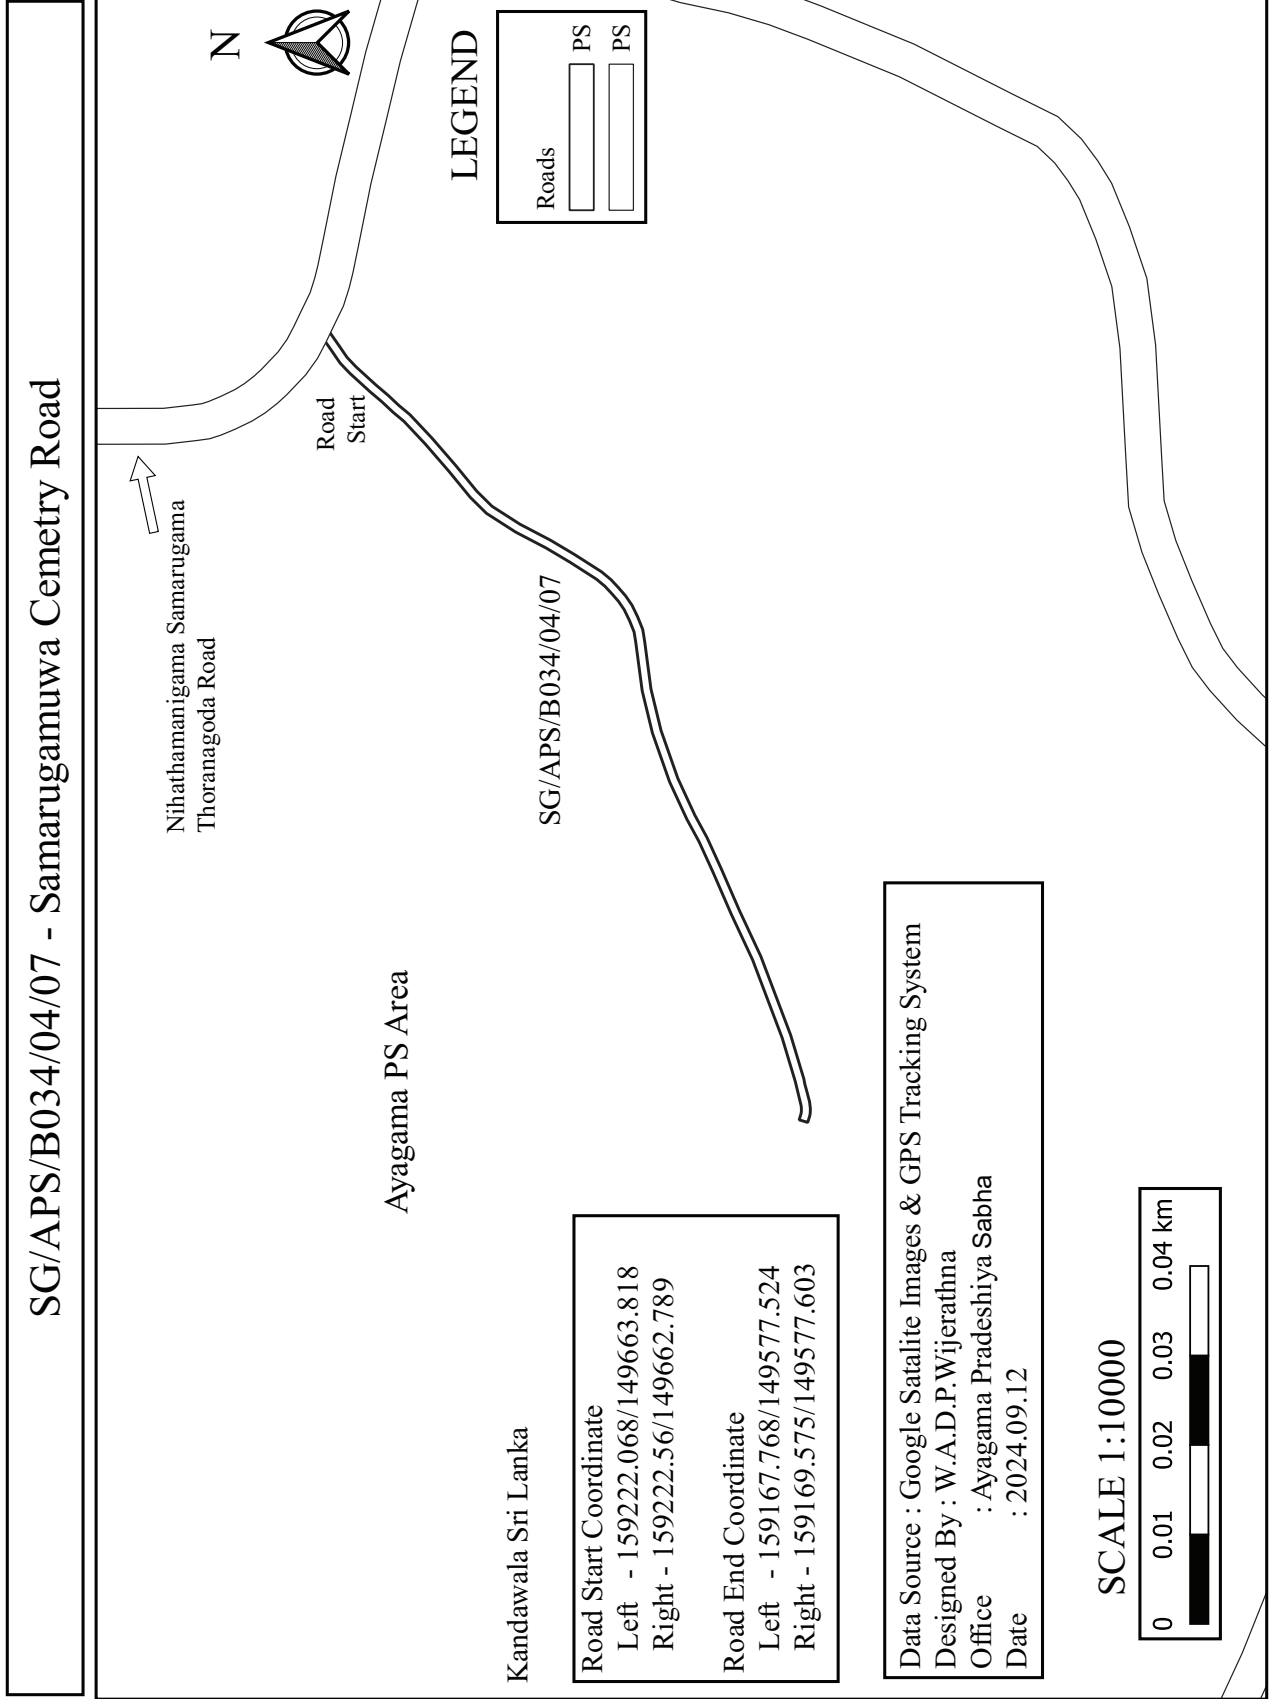

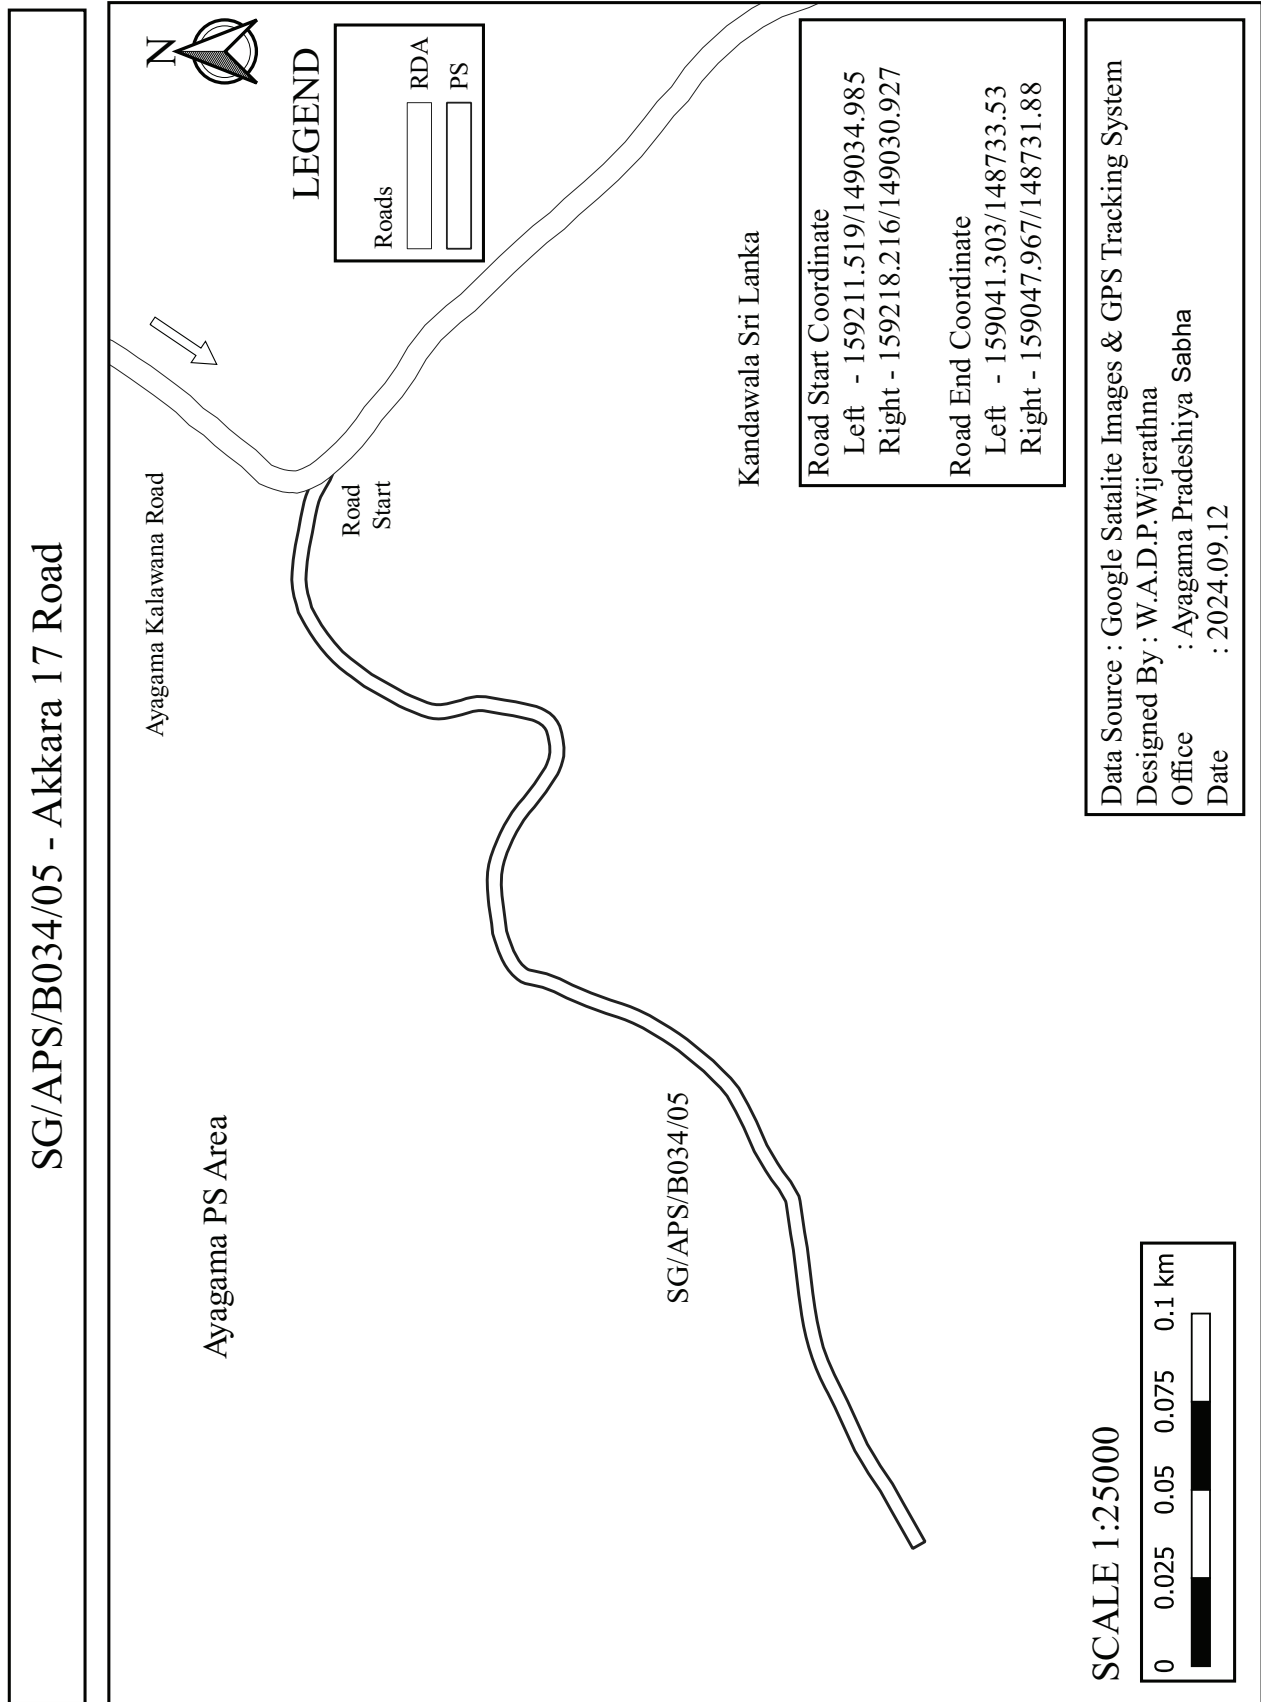


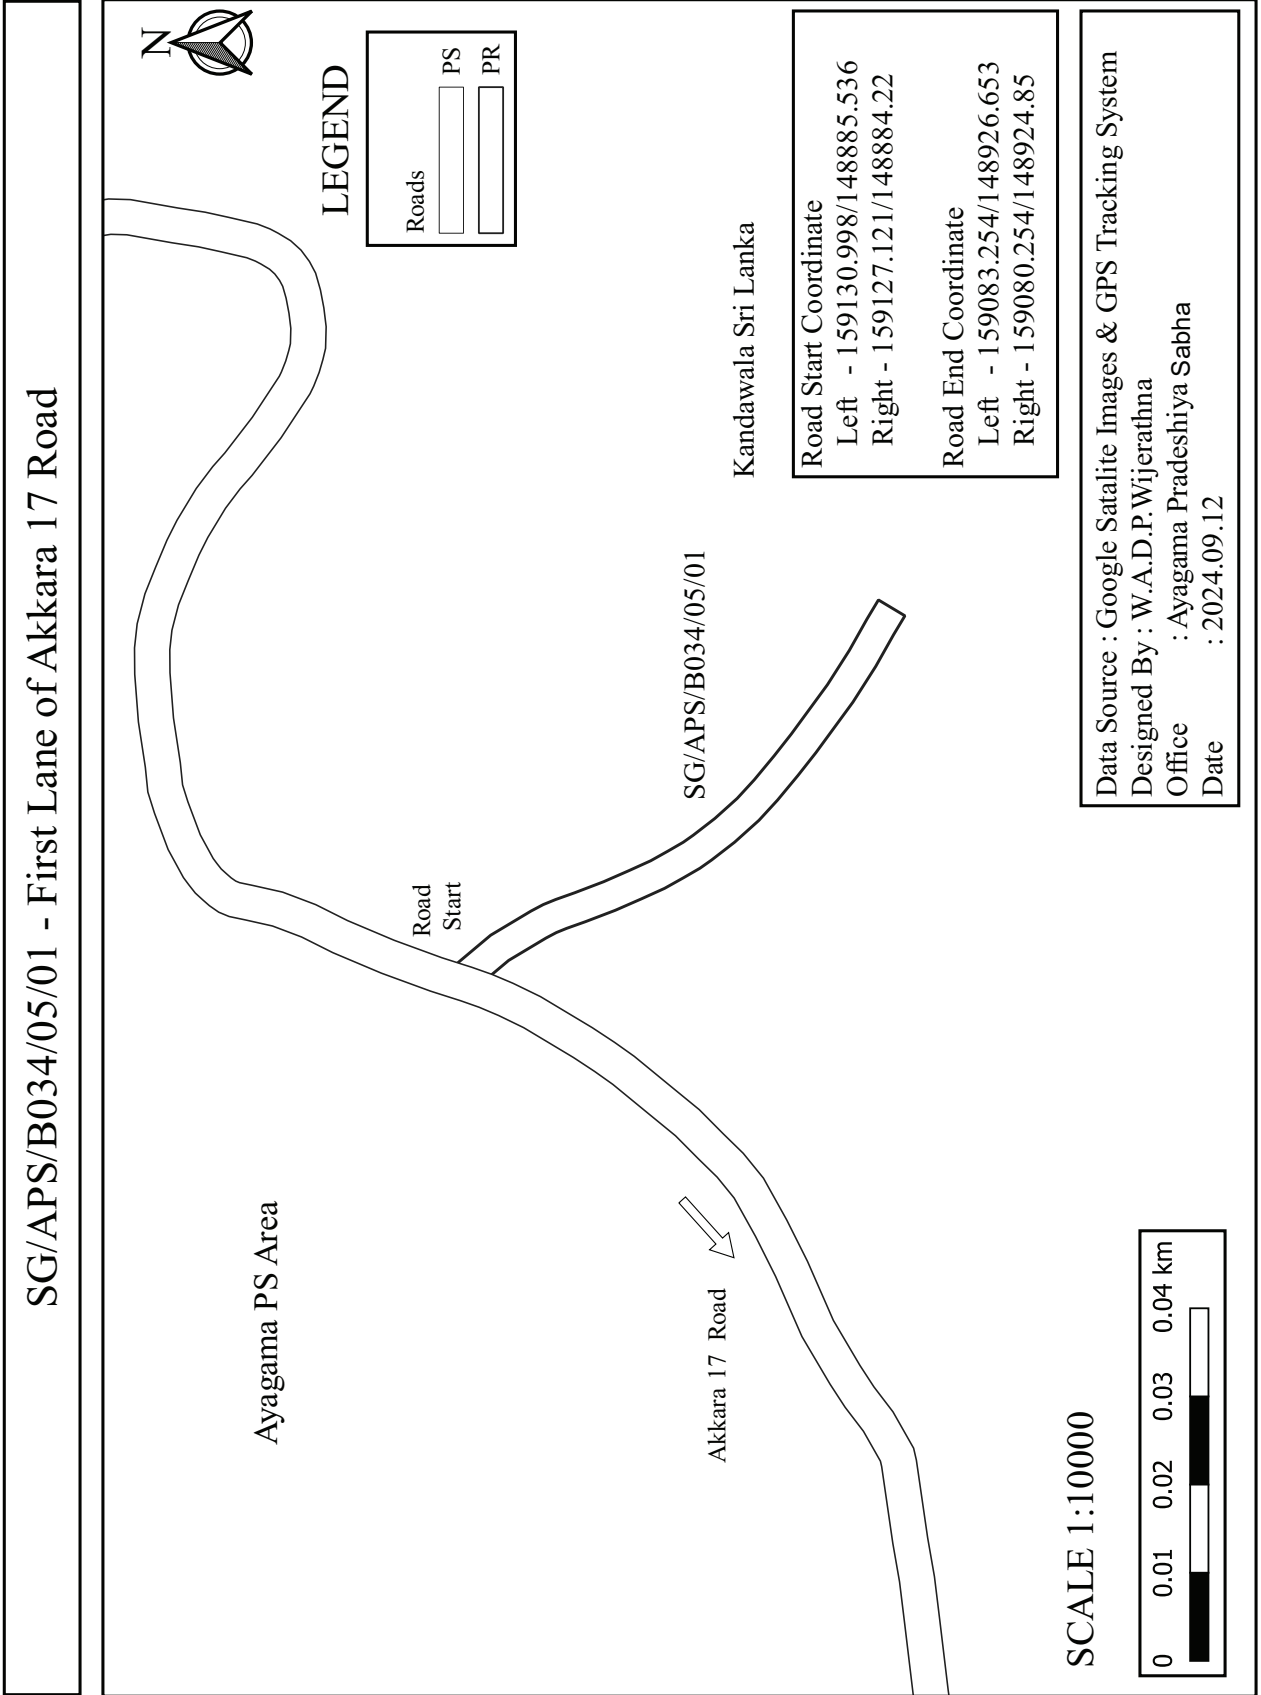


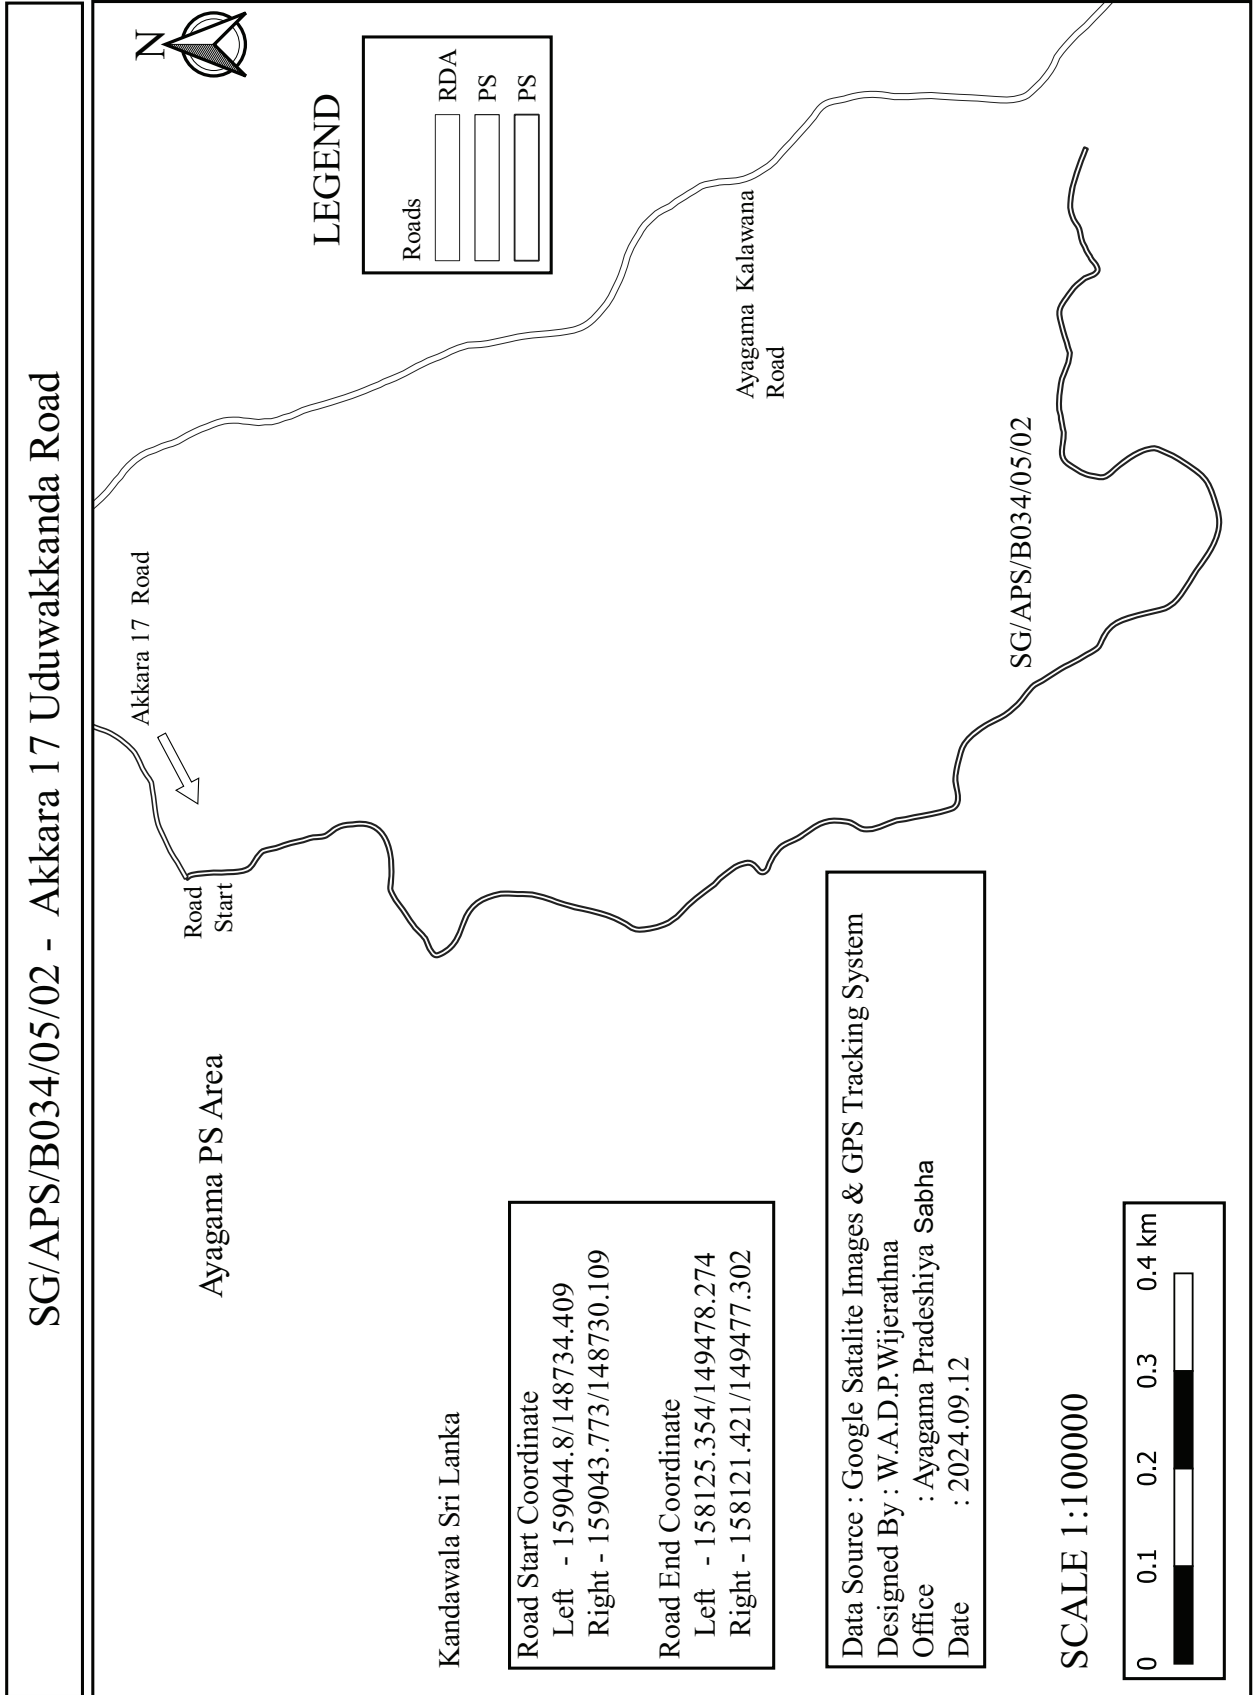


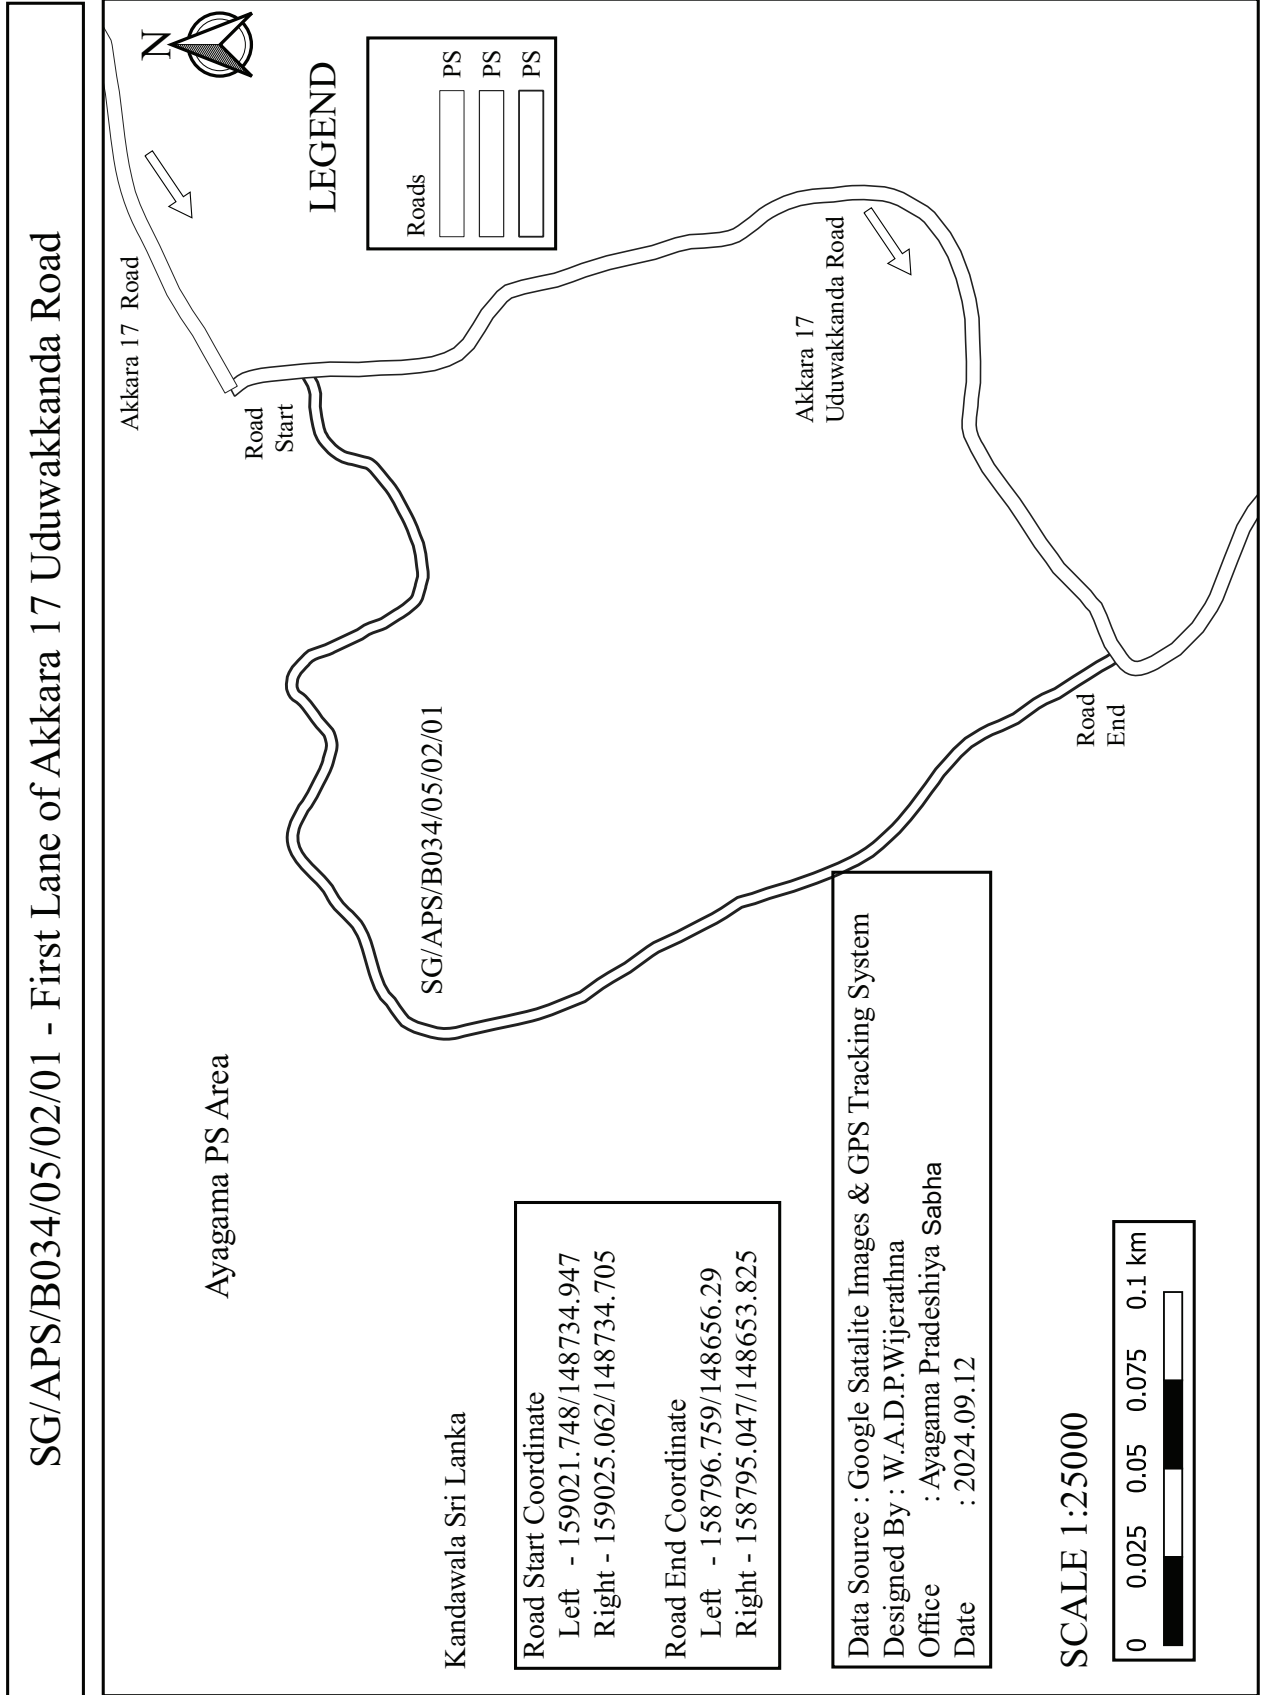


SG/APS/B034/05/02/01/01 - First By Pass of Akkara 17 Uduwakkanda Road

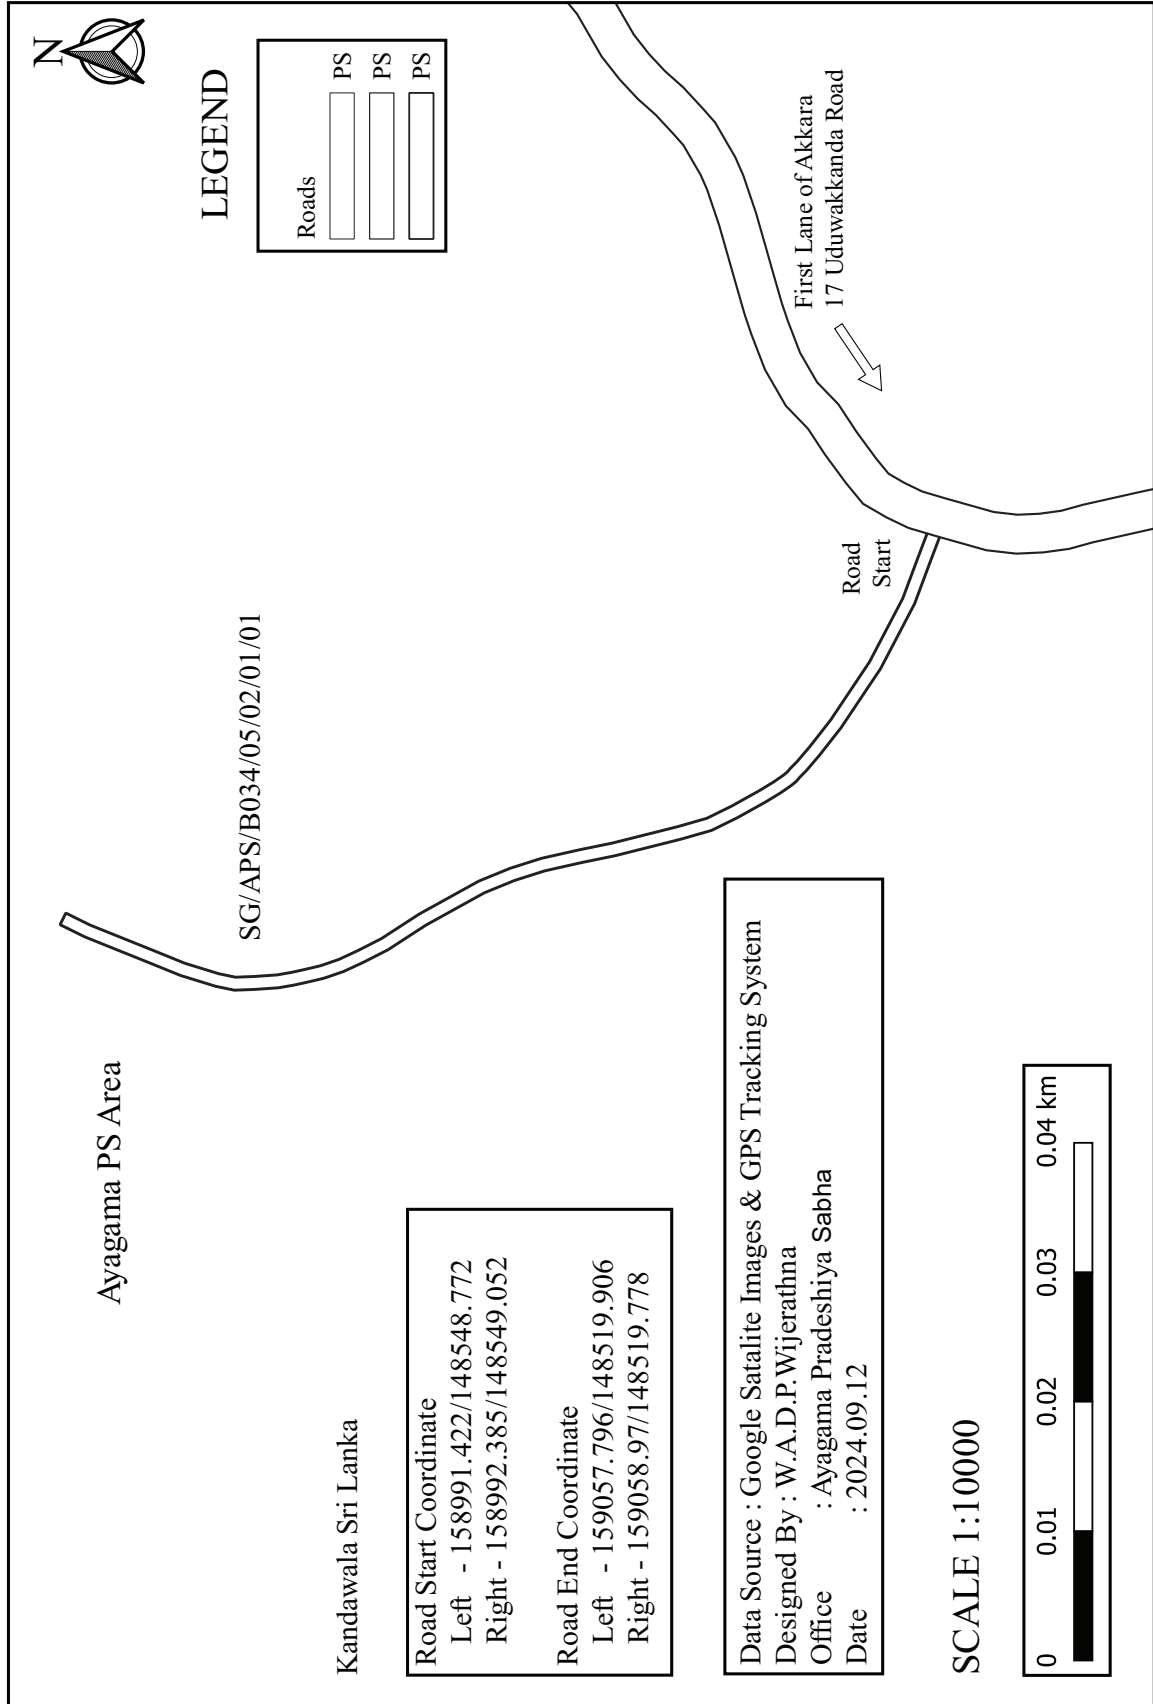


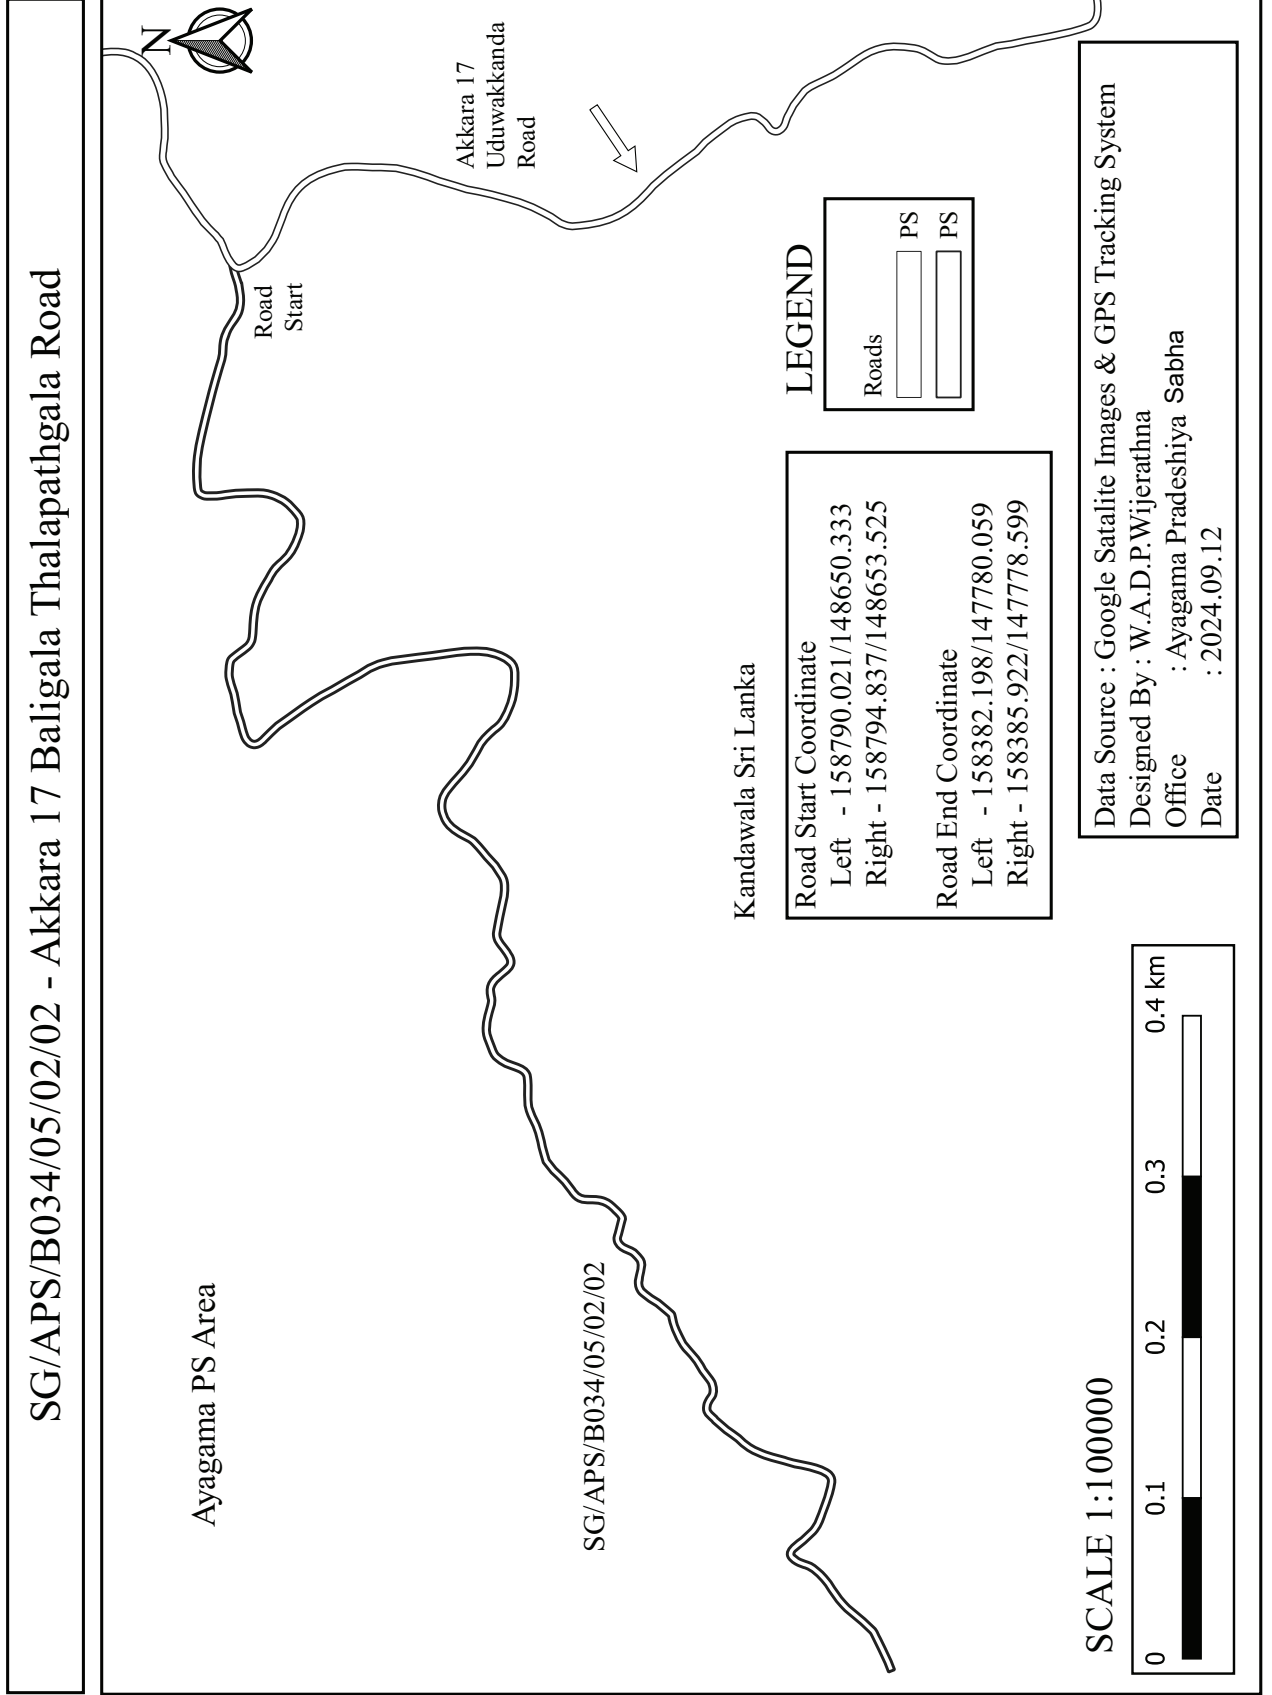


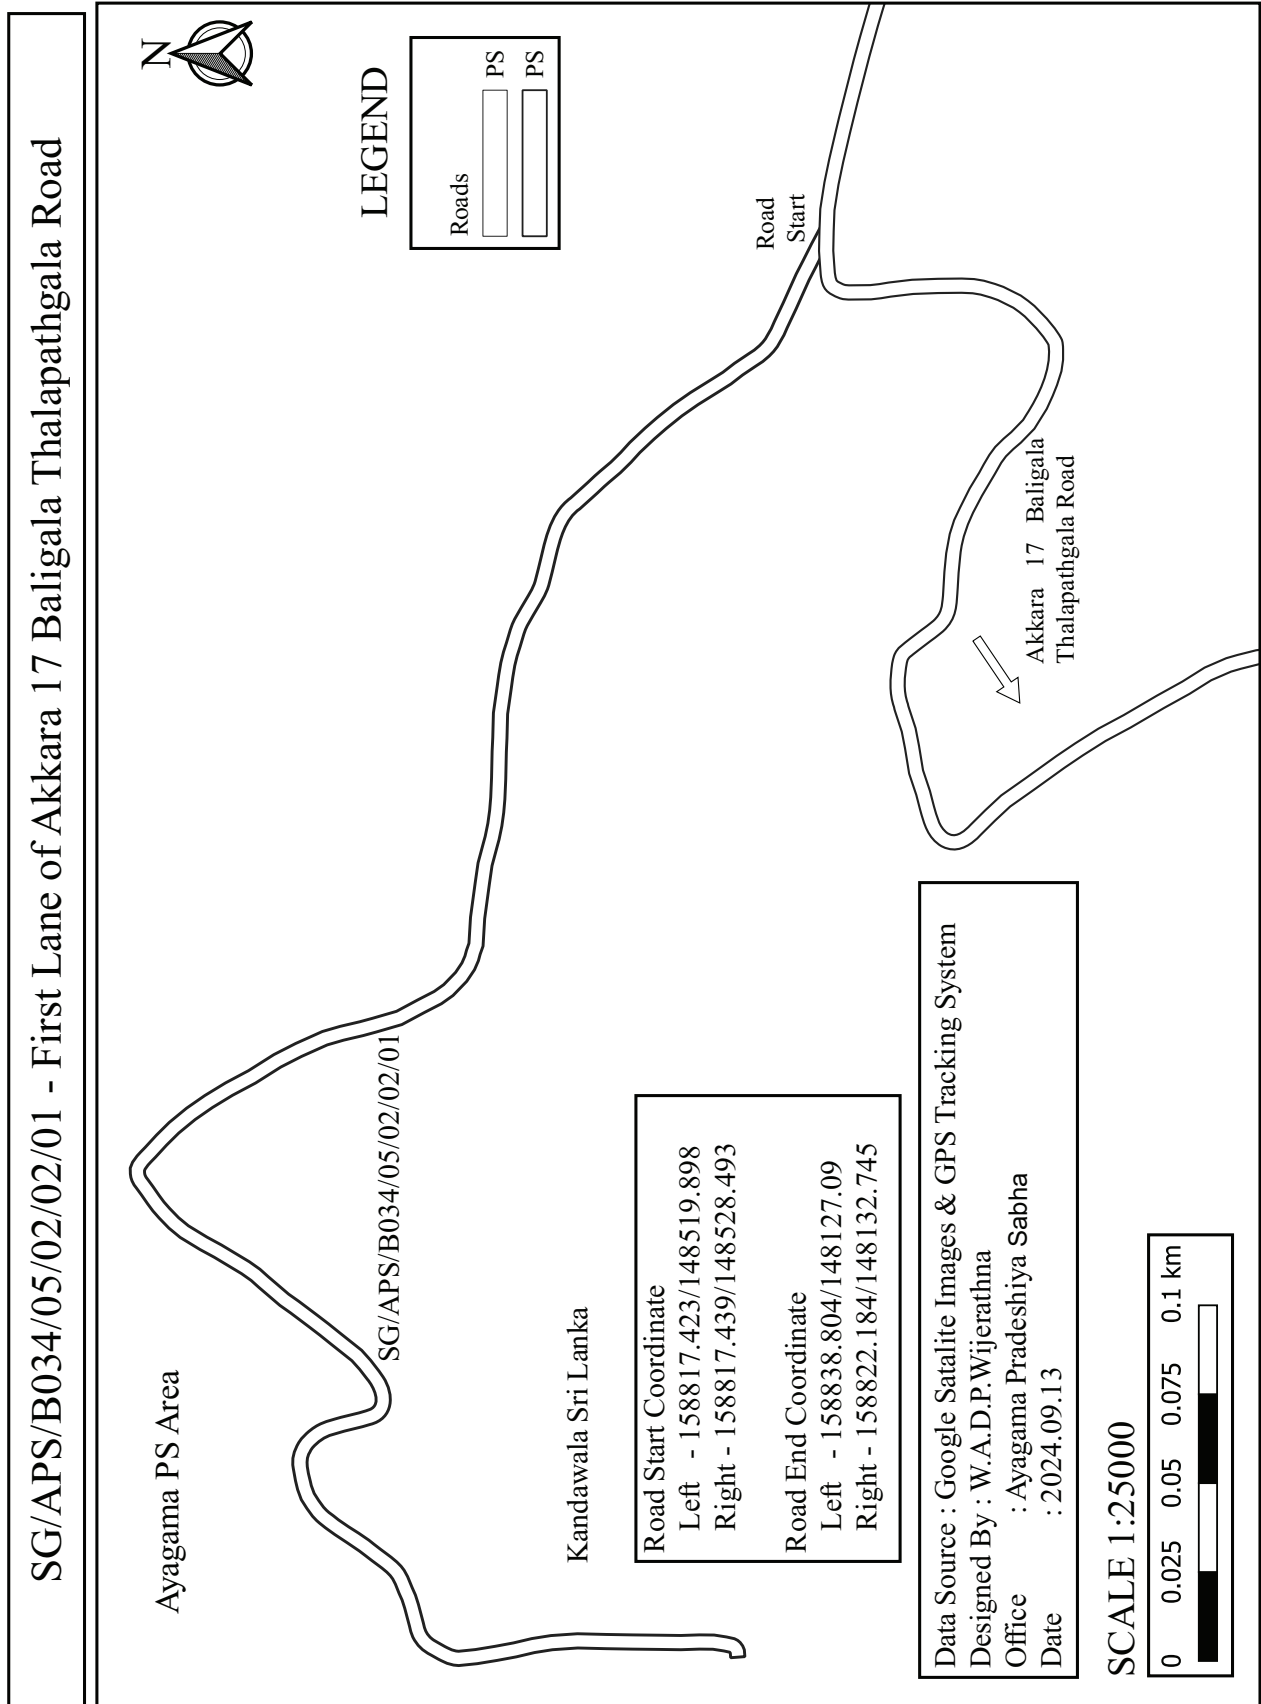


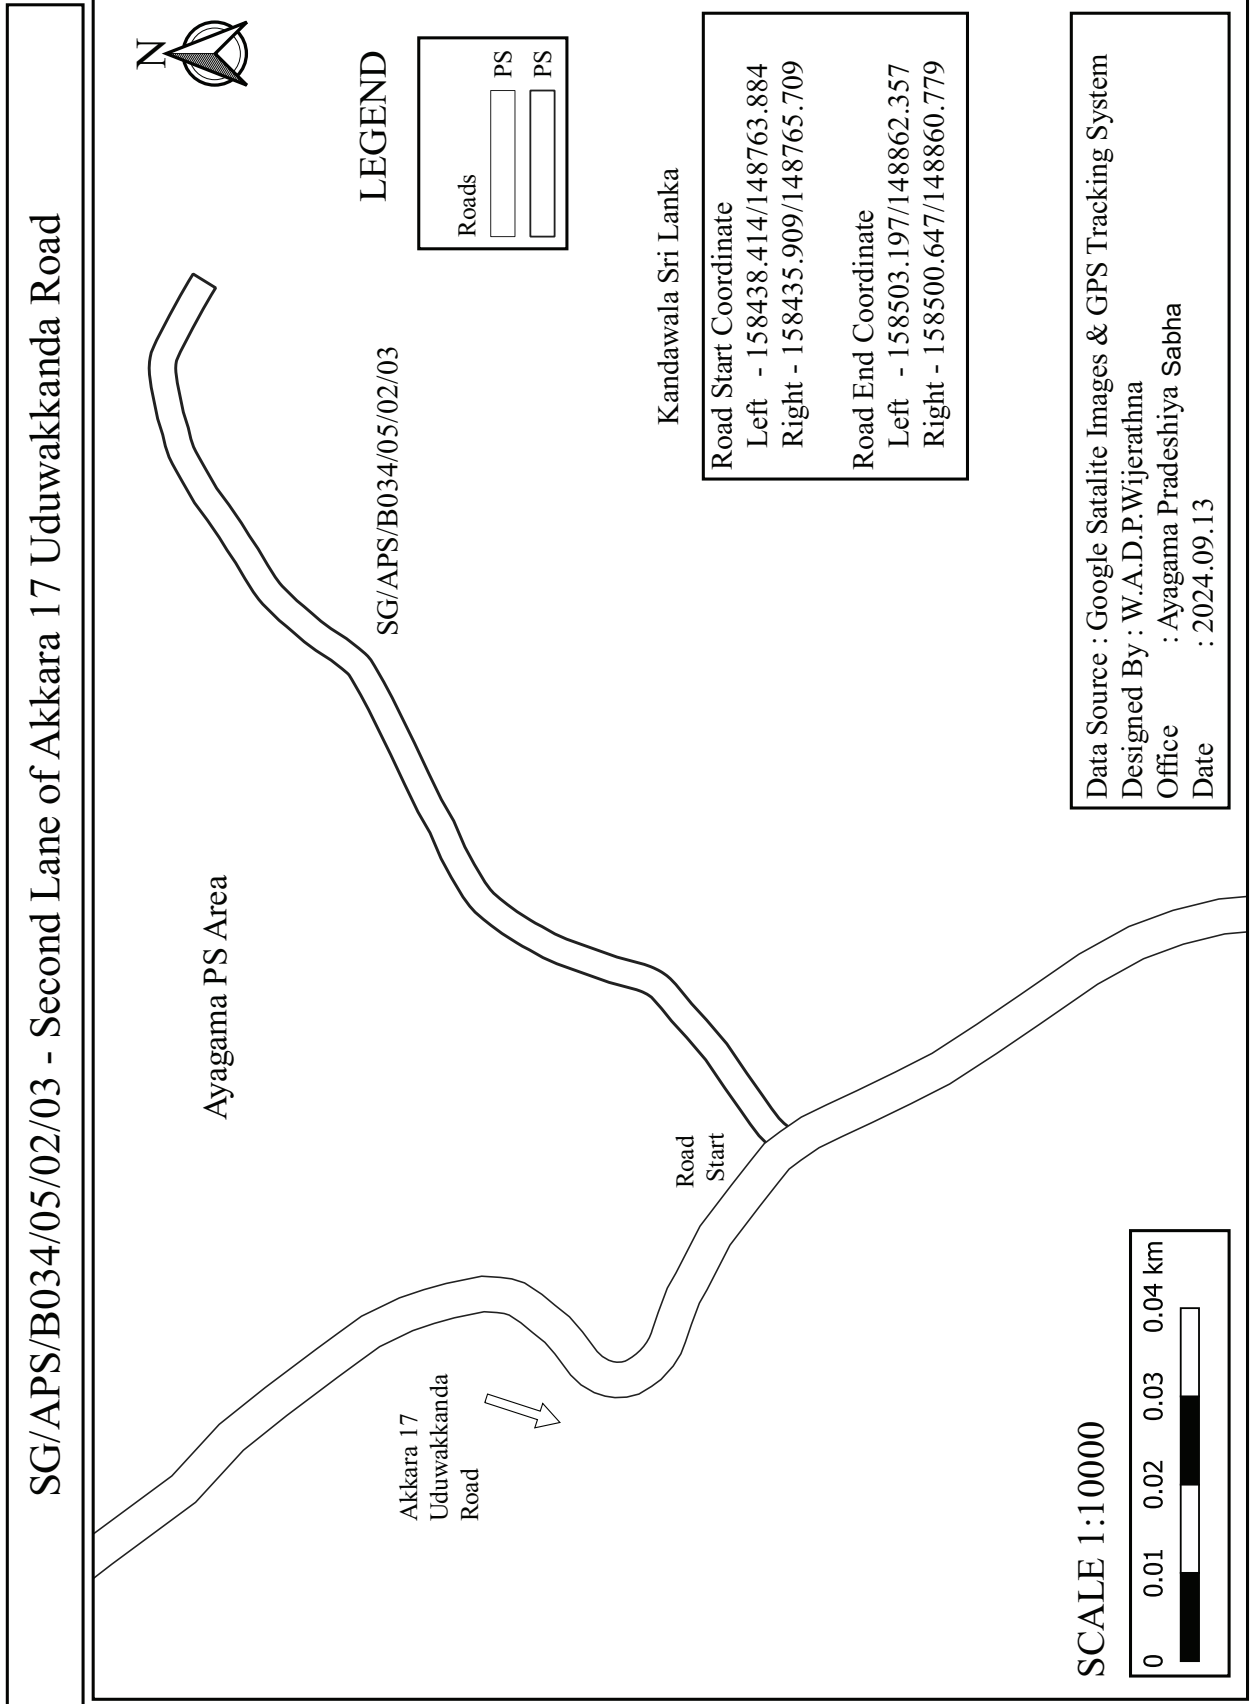



SG/APS/B034/06 -Ereporuwa First Lane

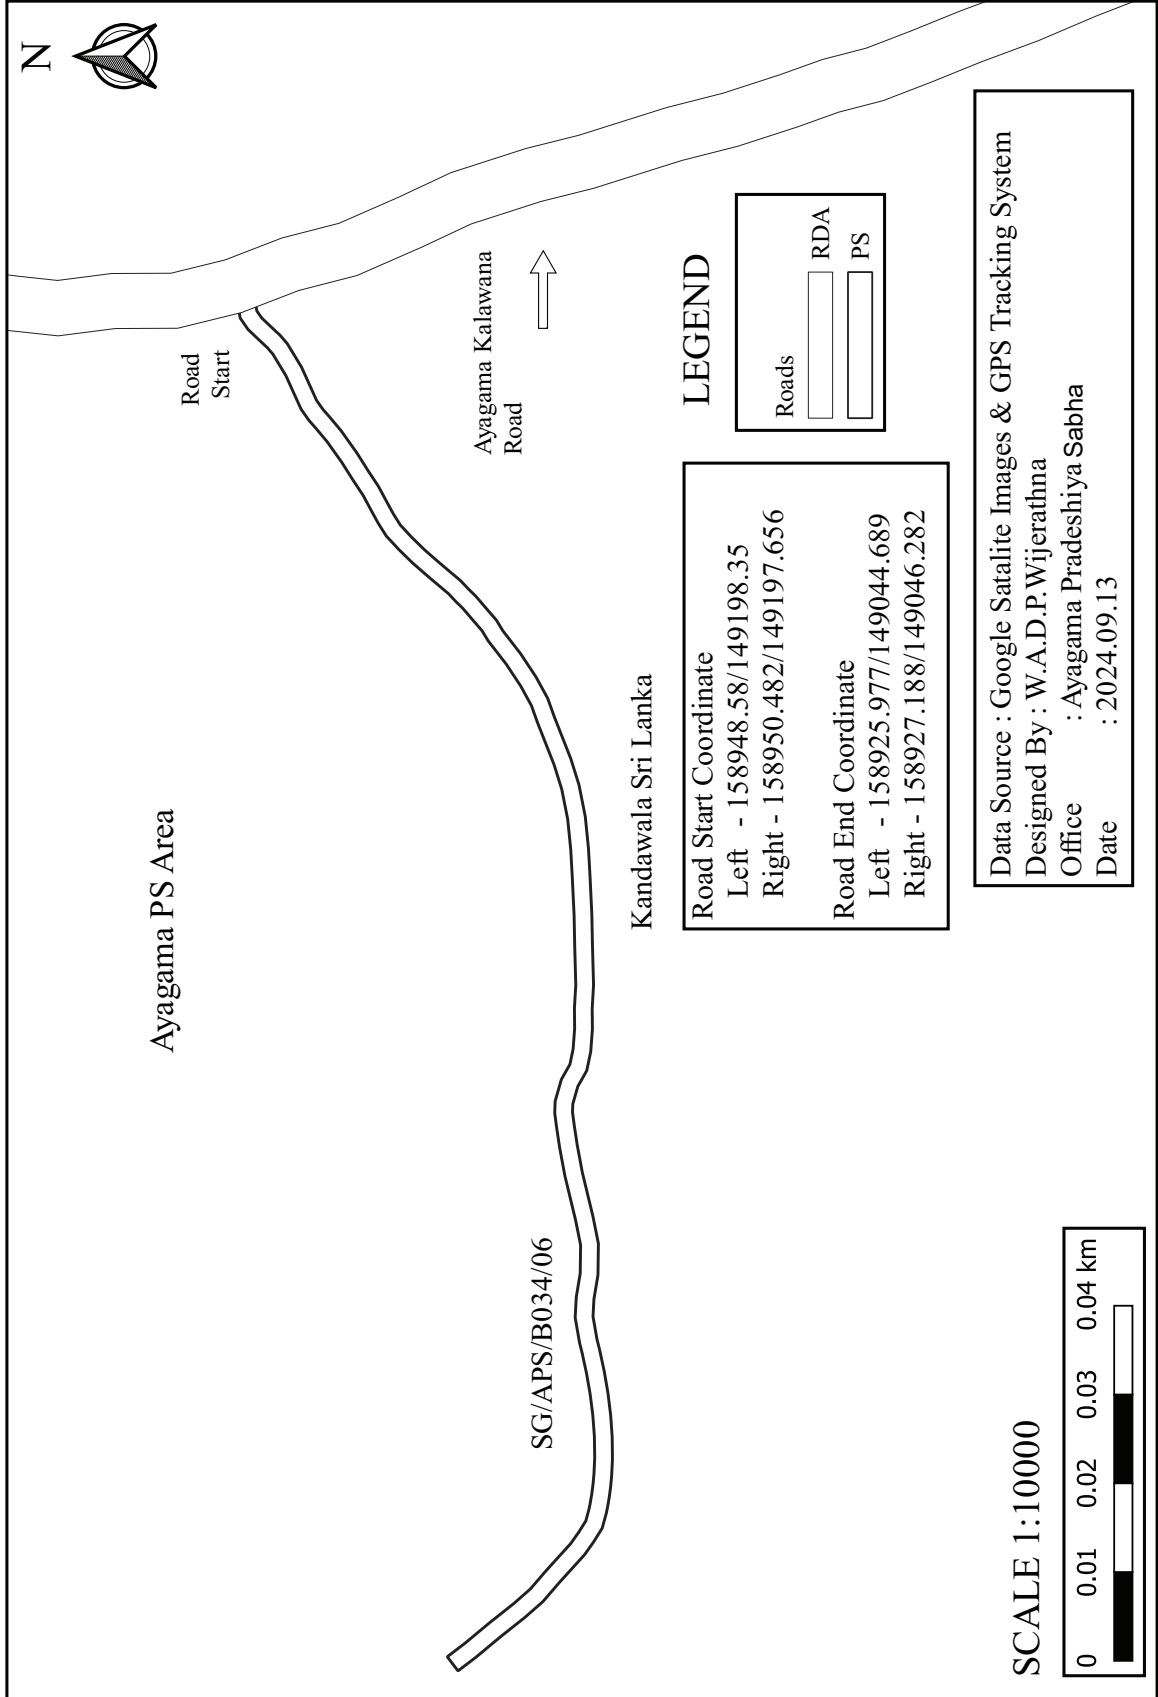


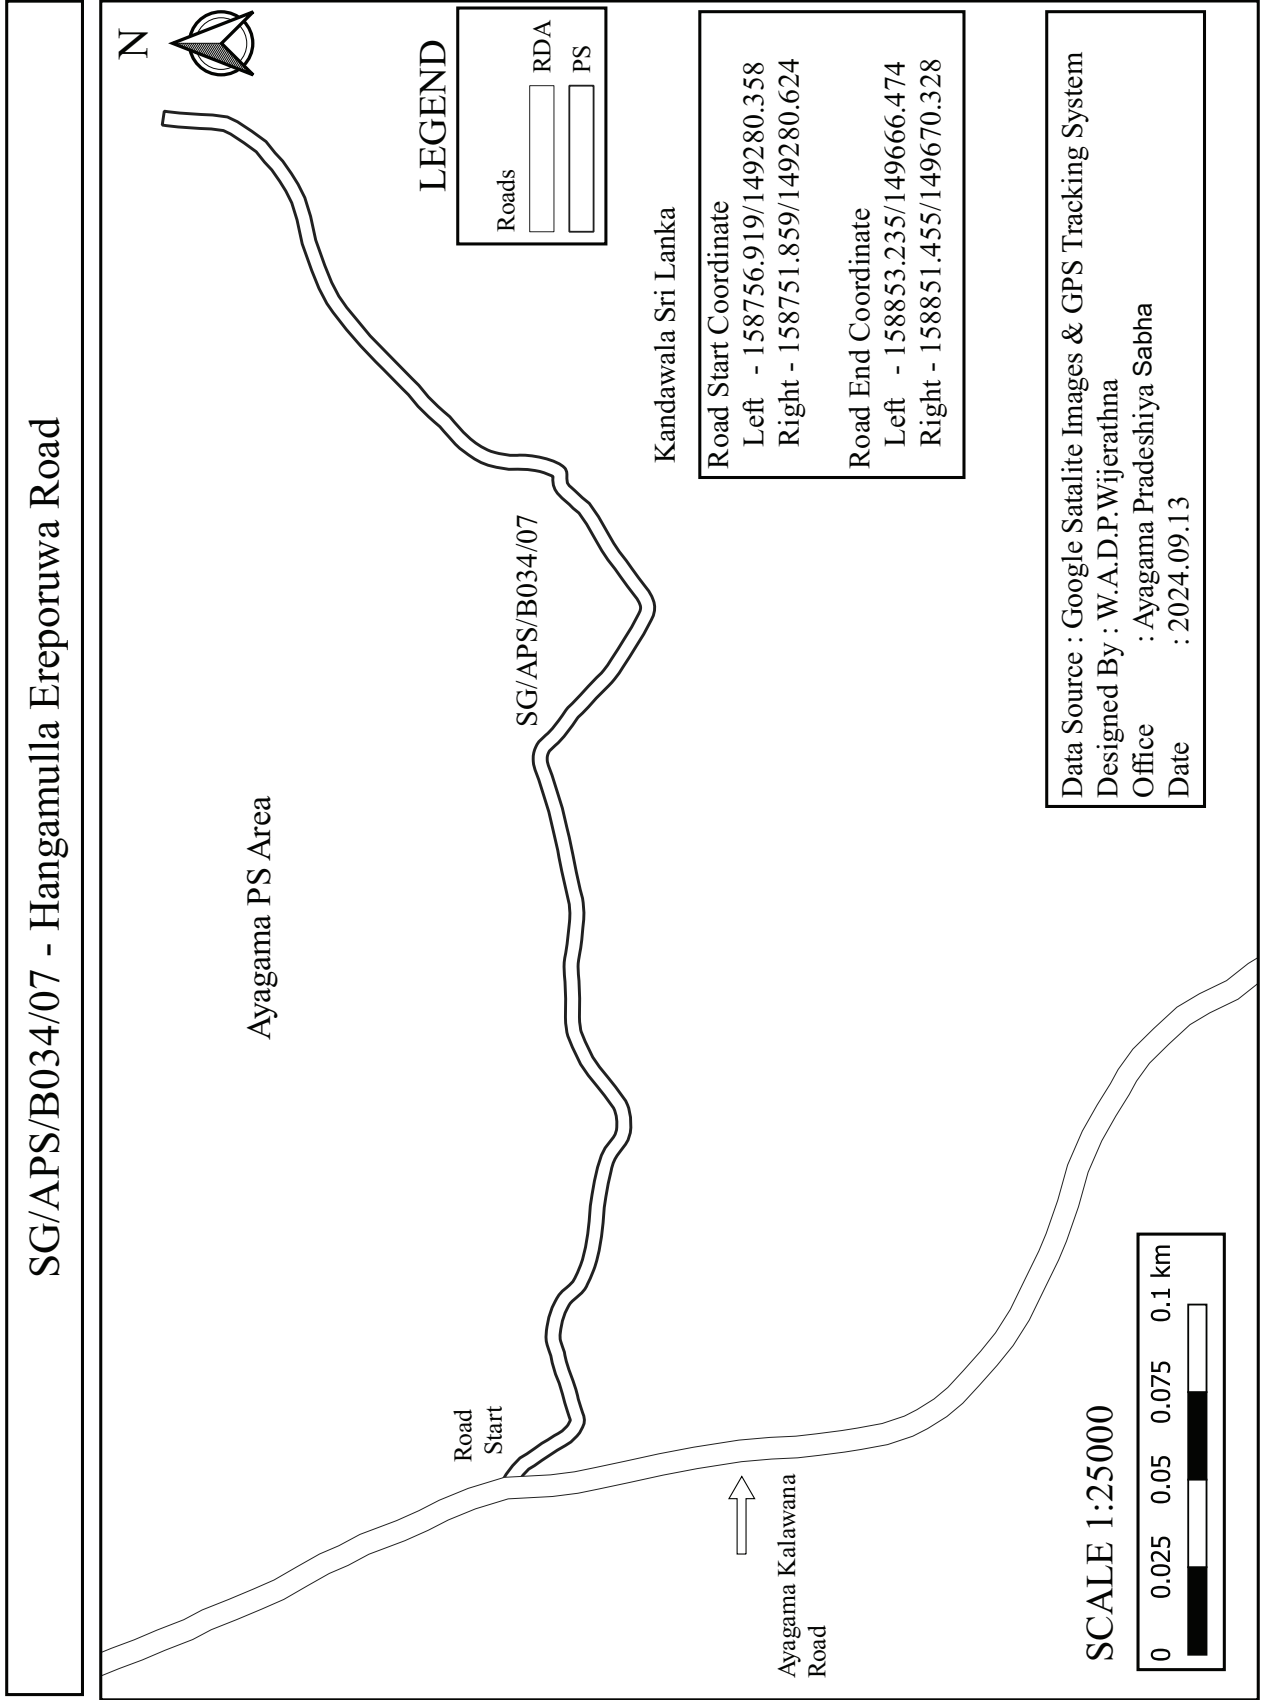


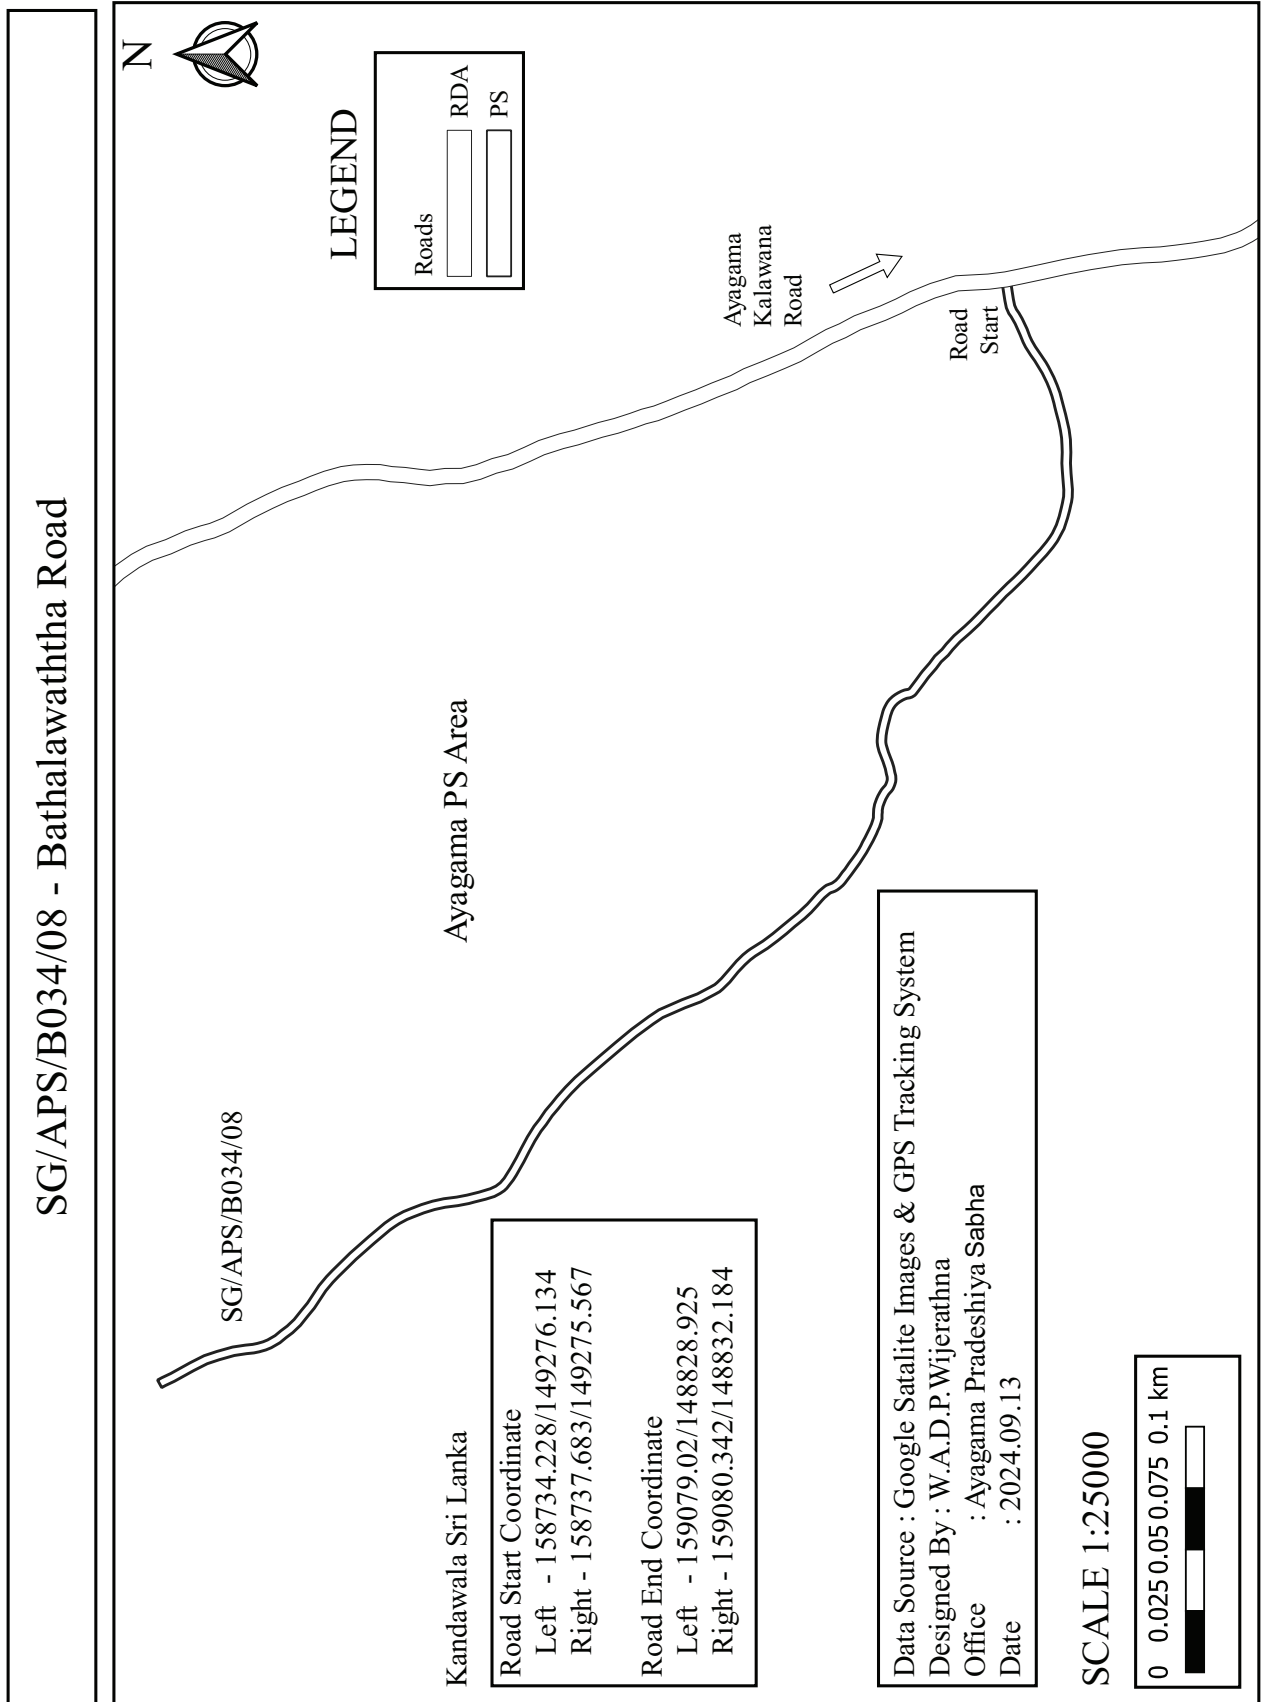


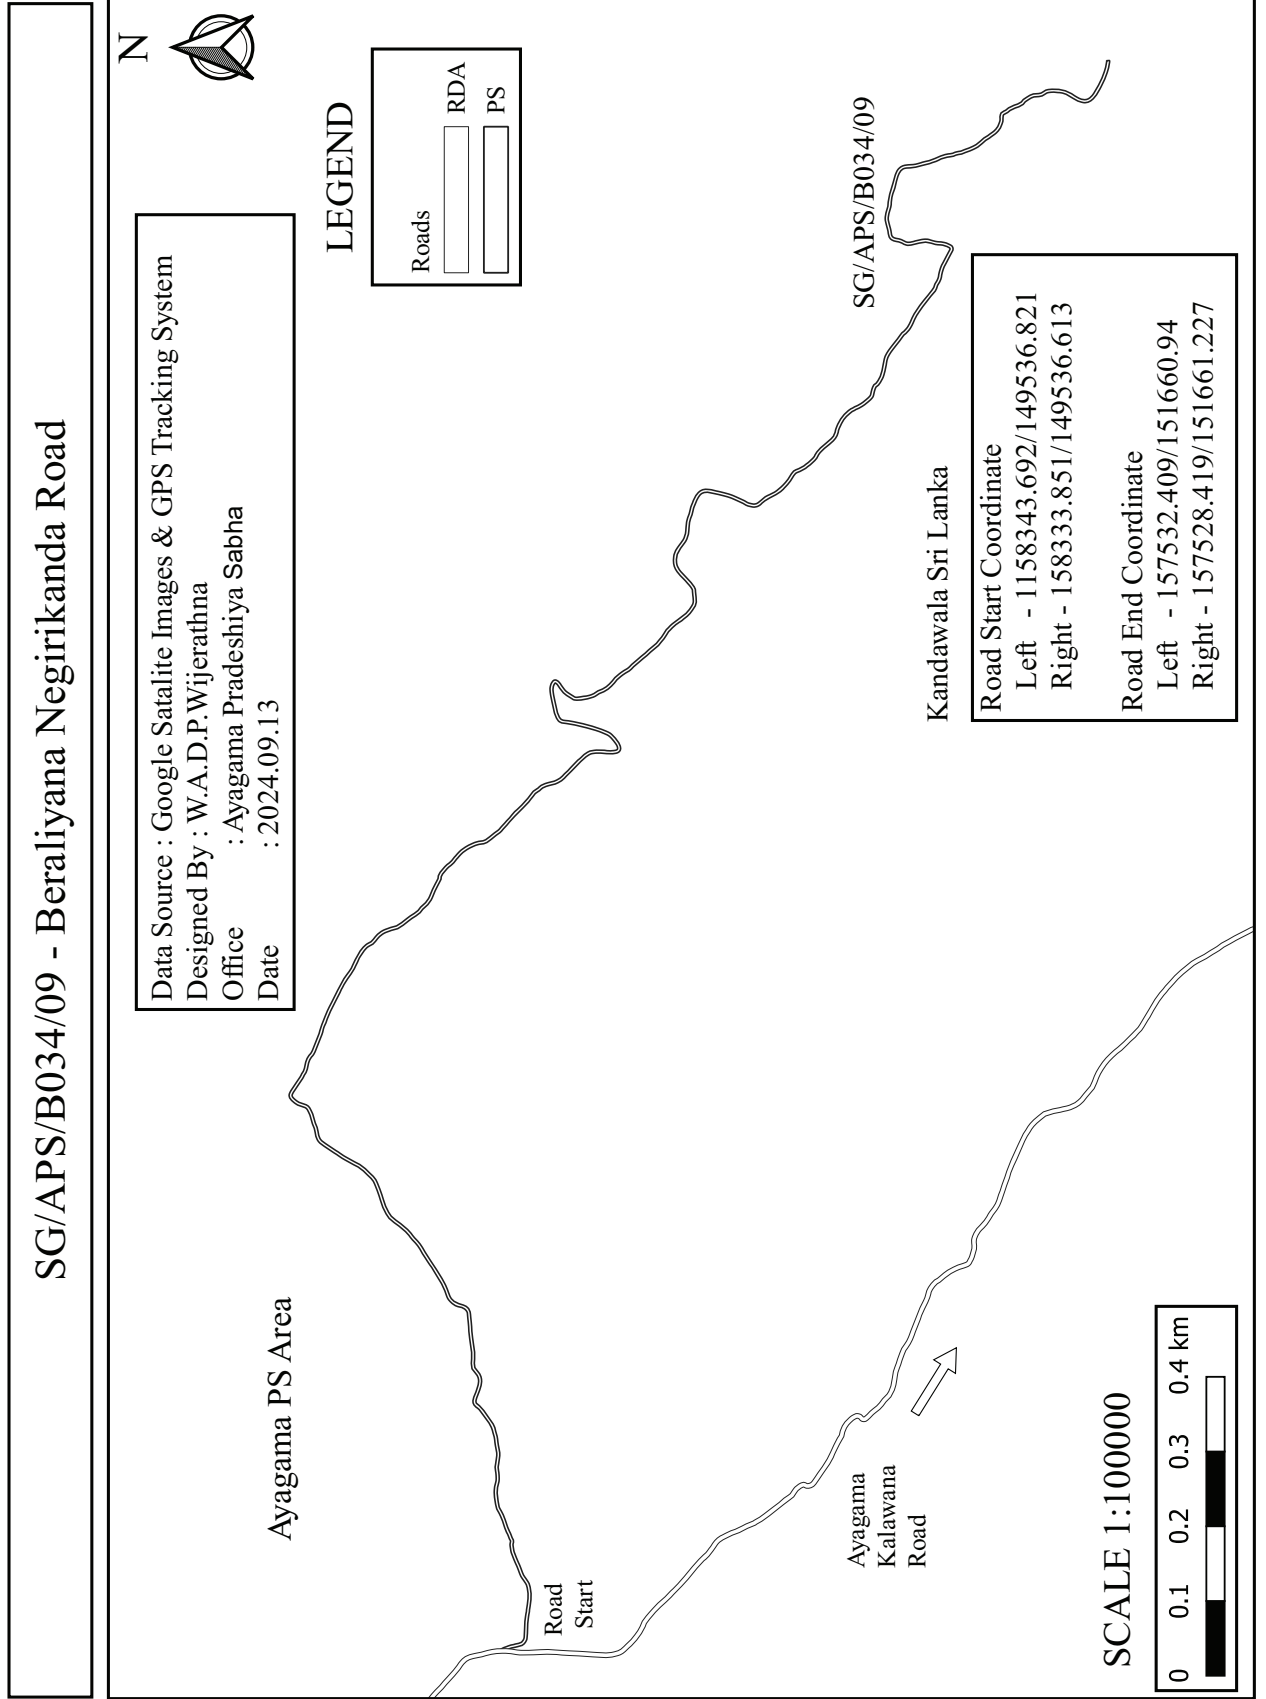


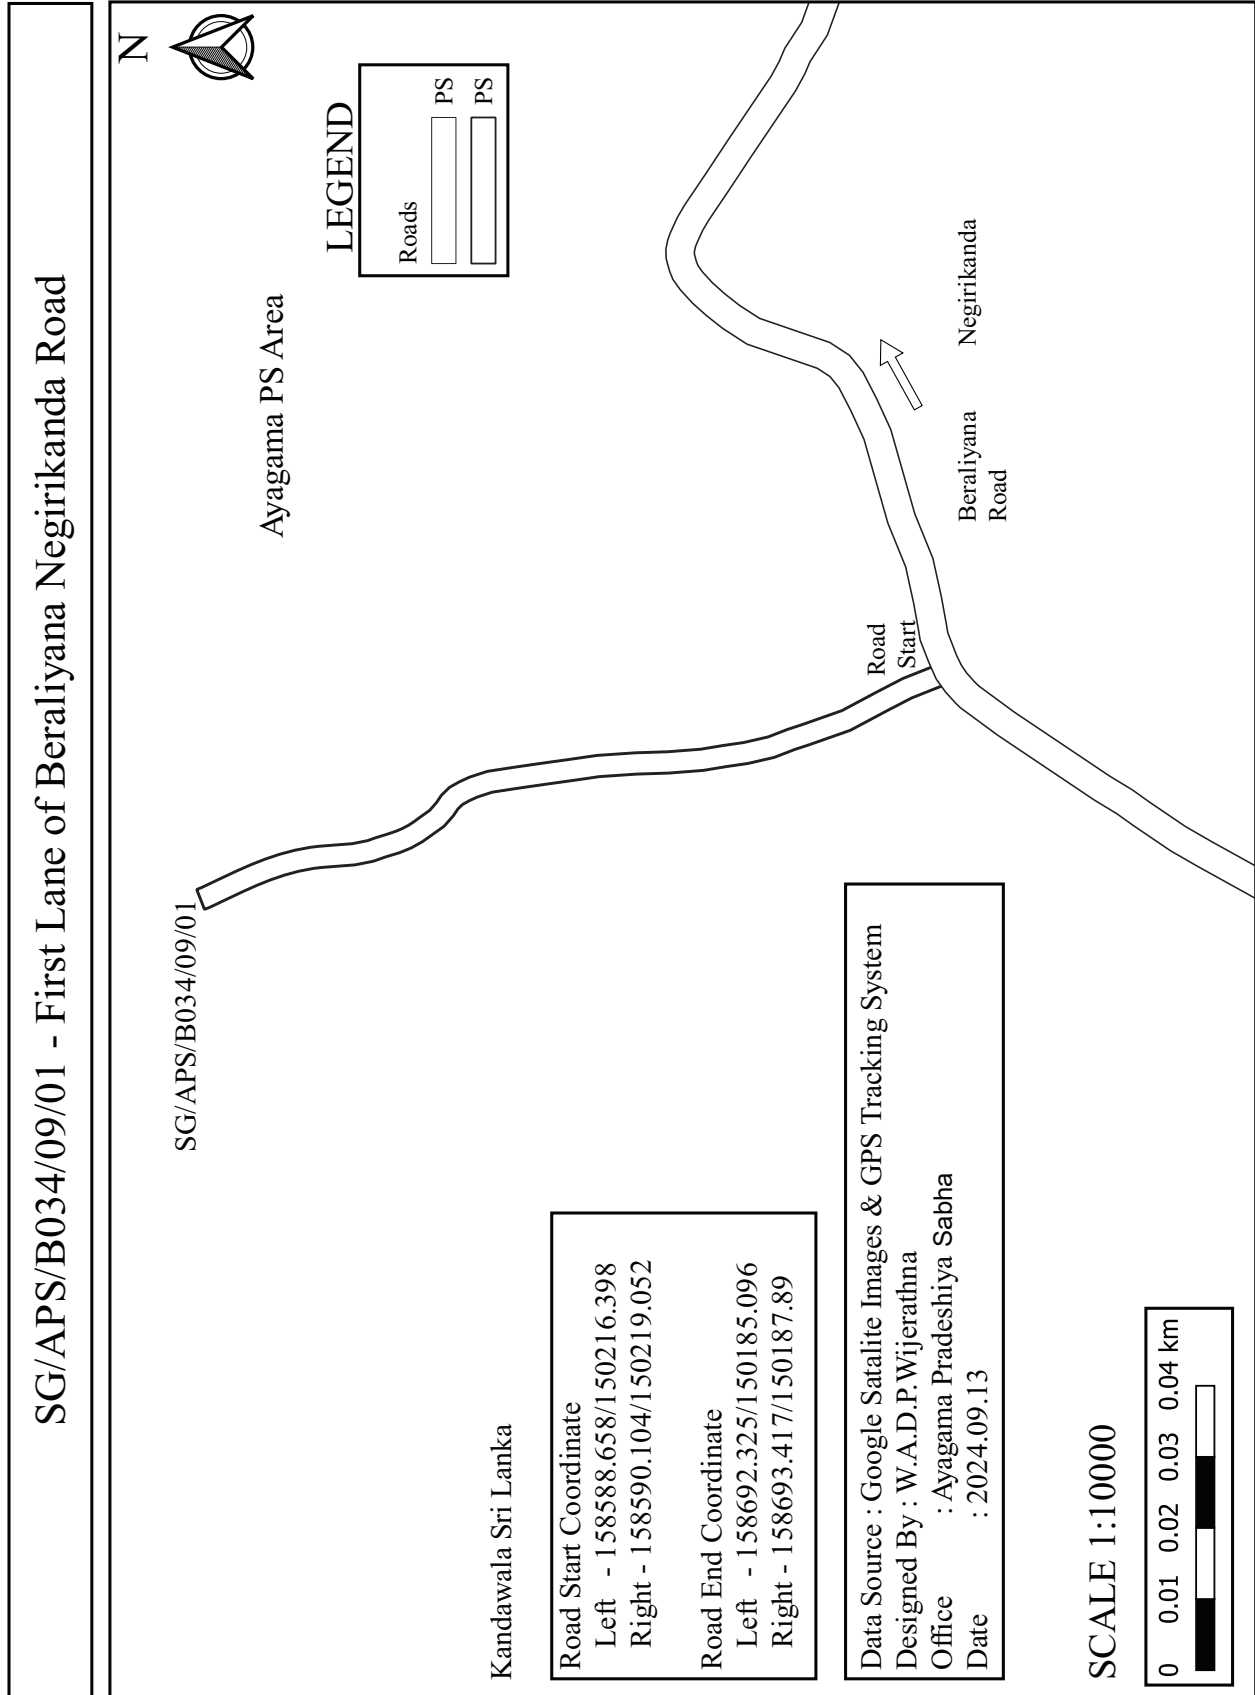


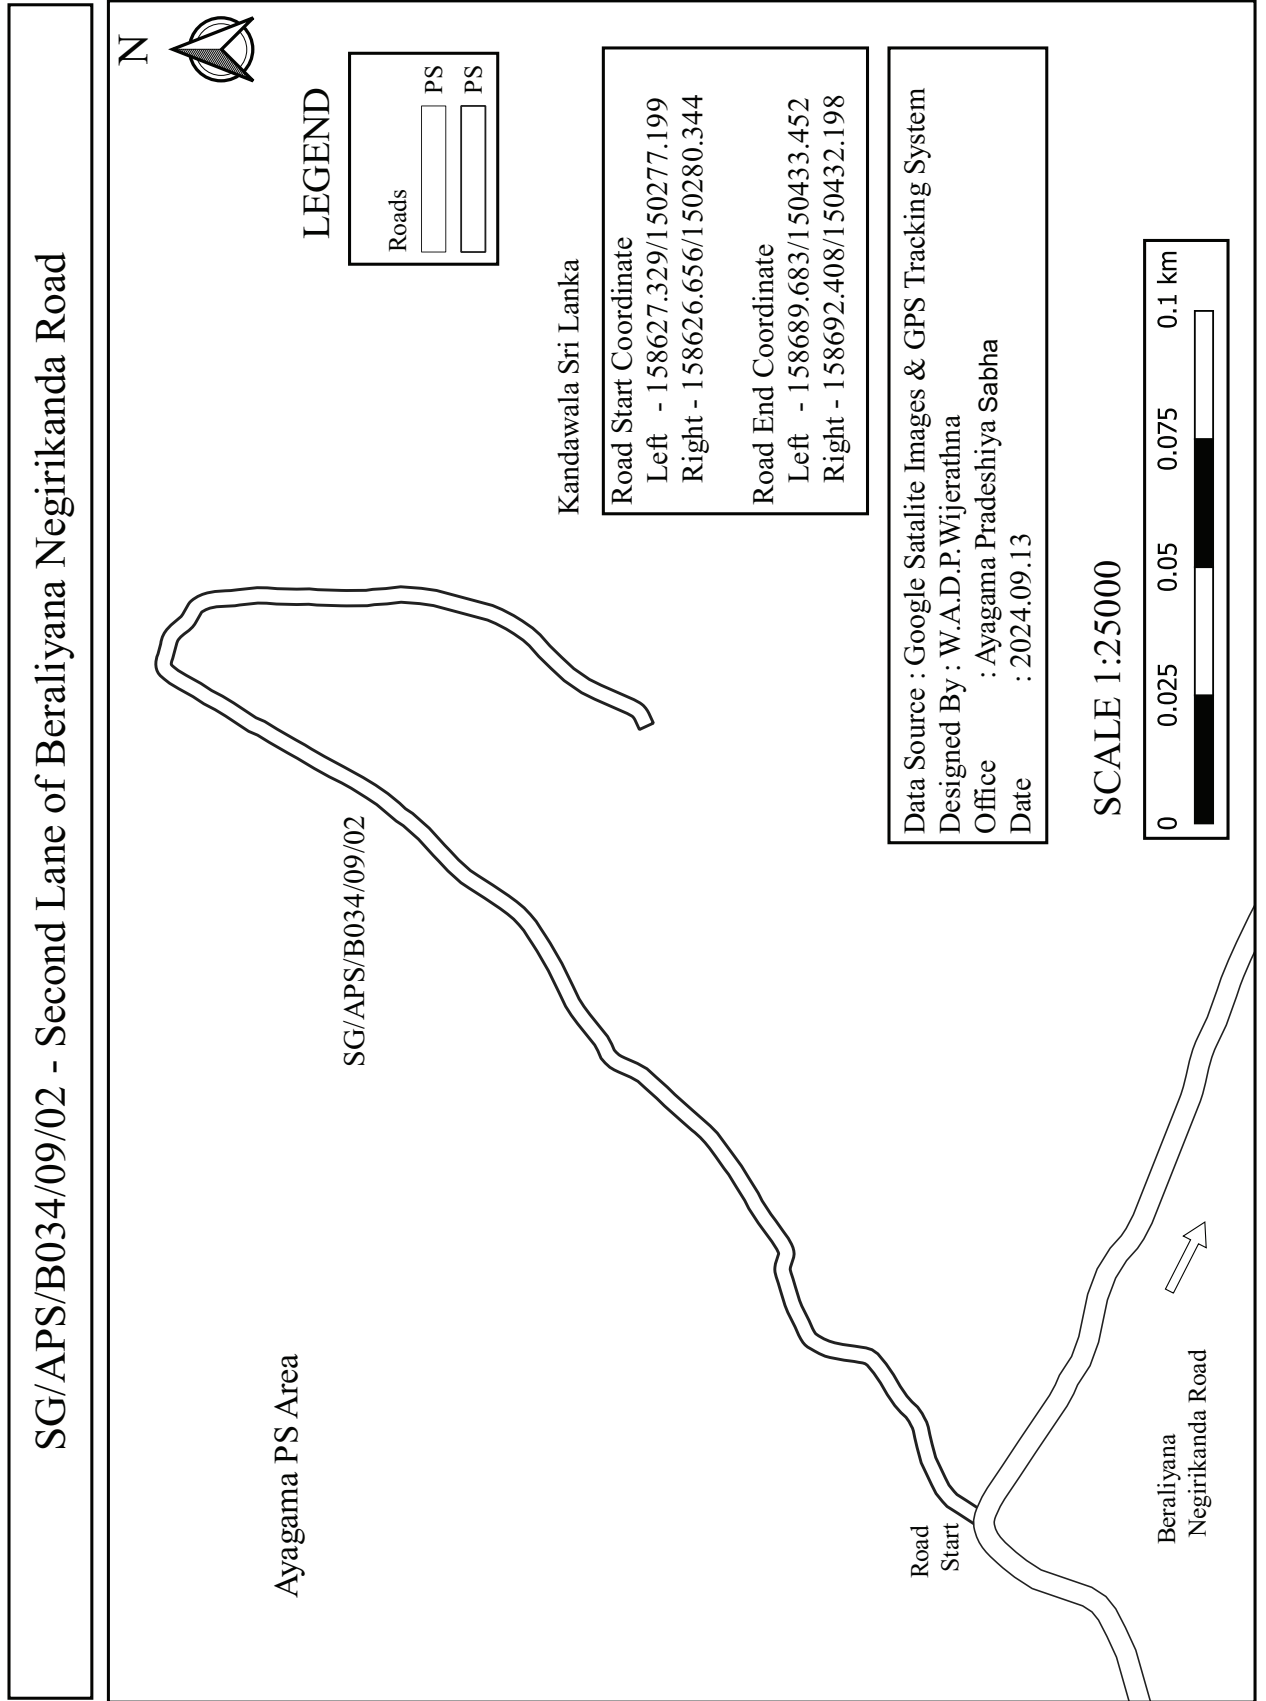


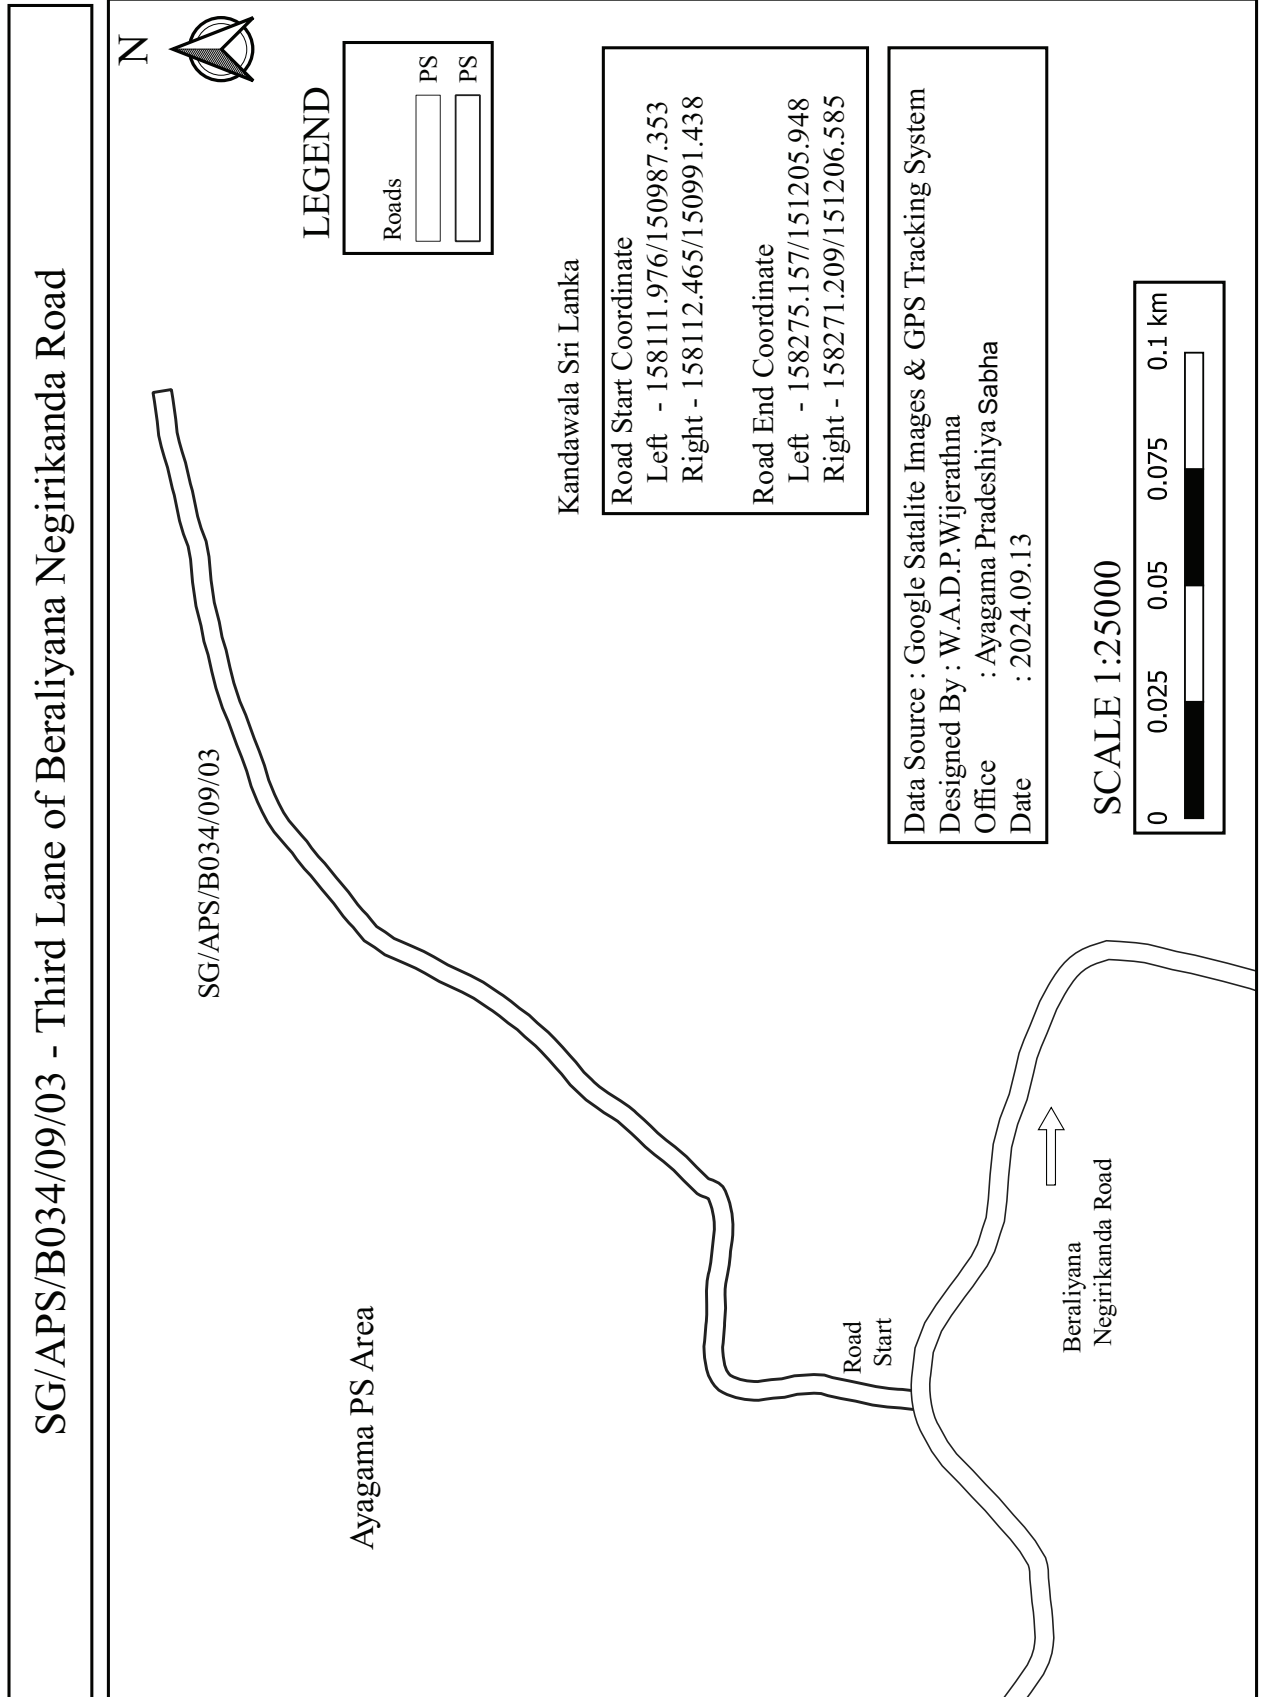


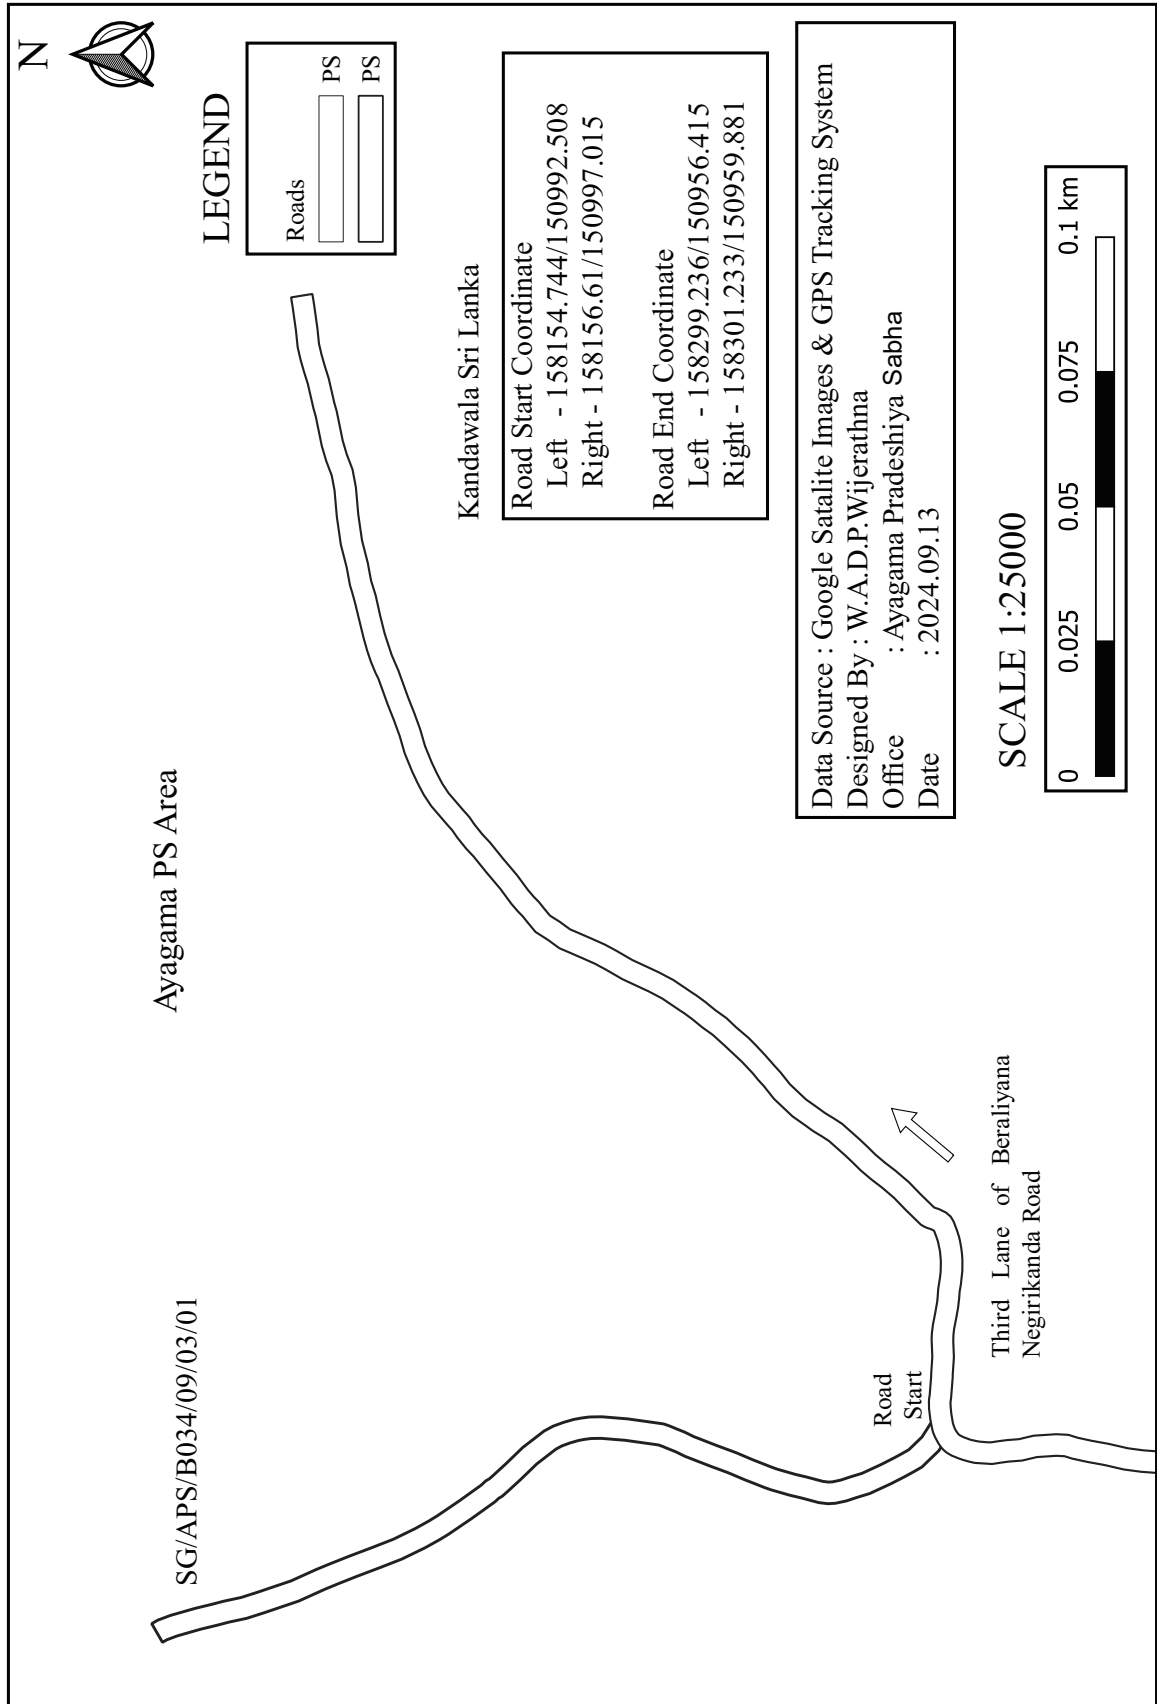


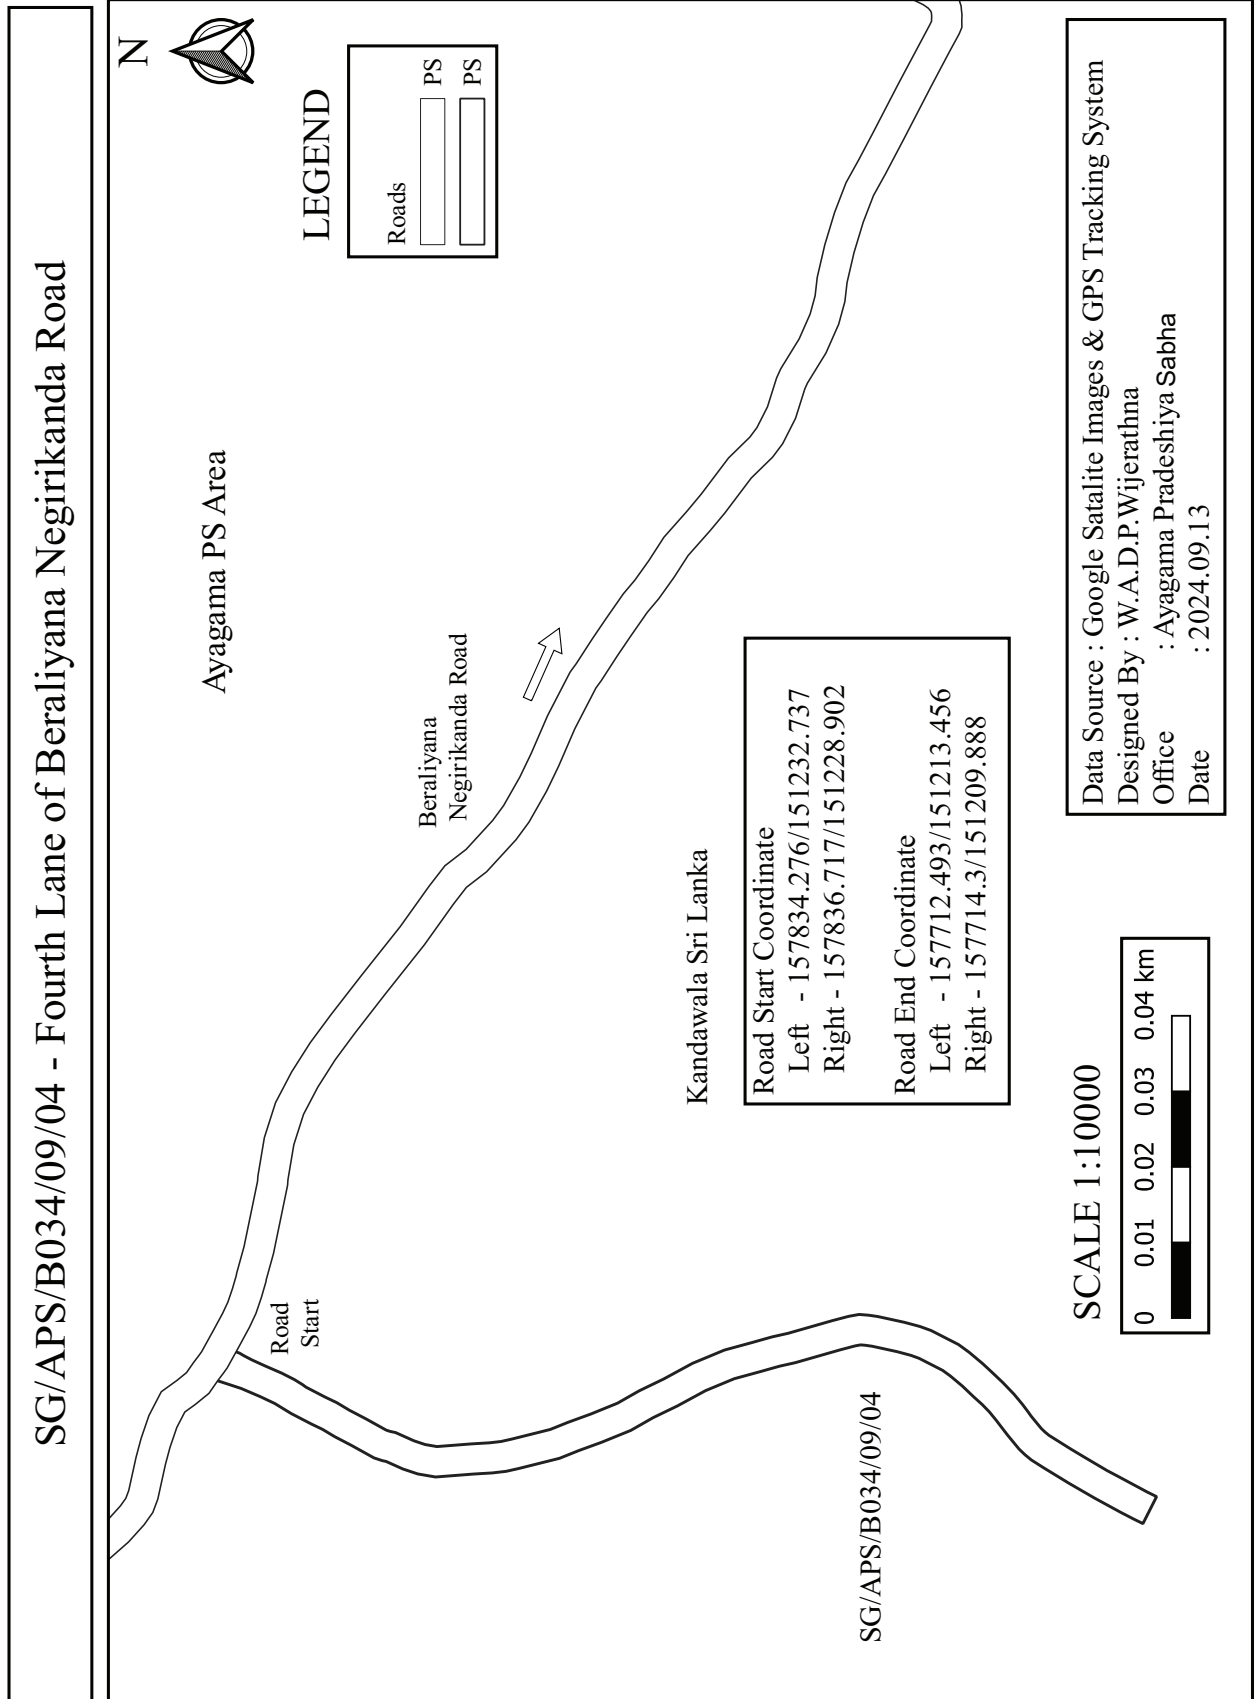


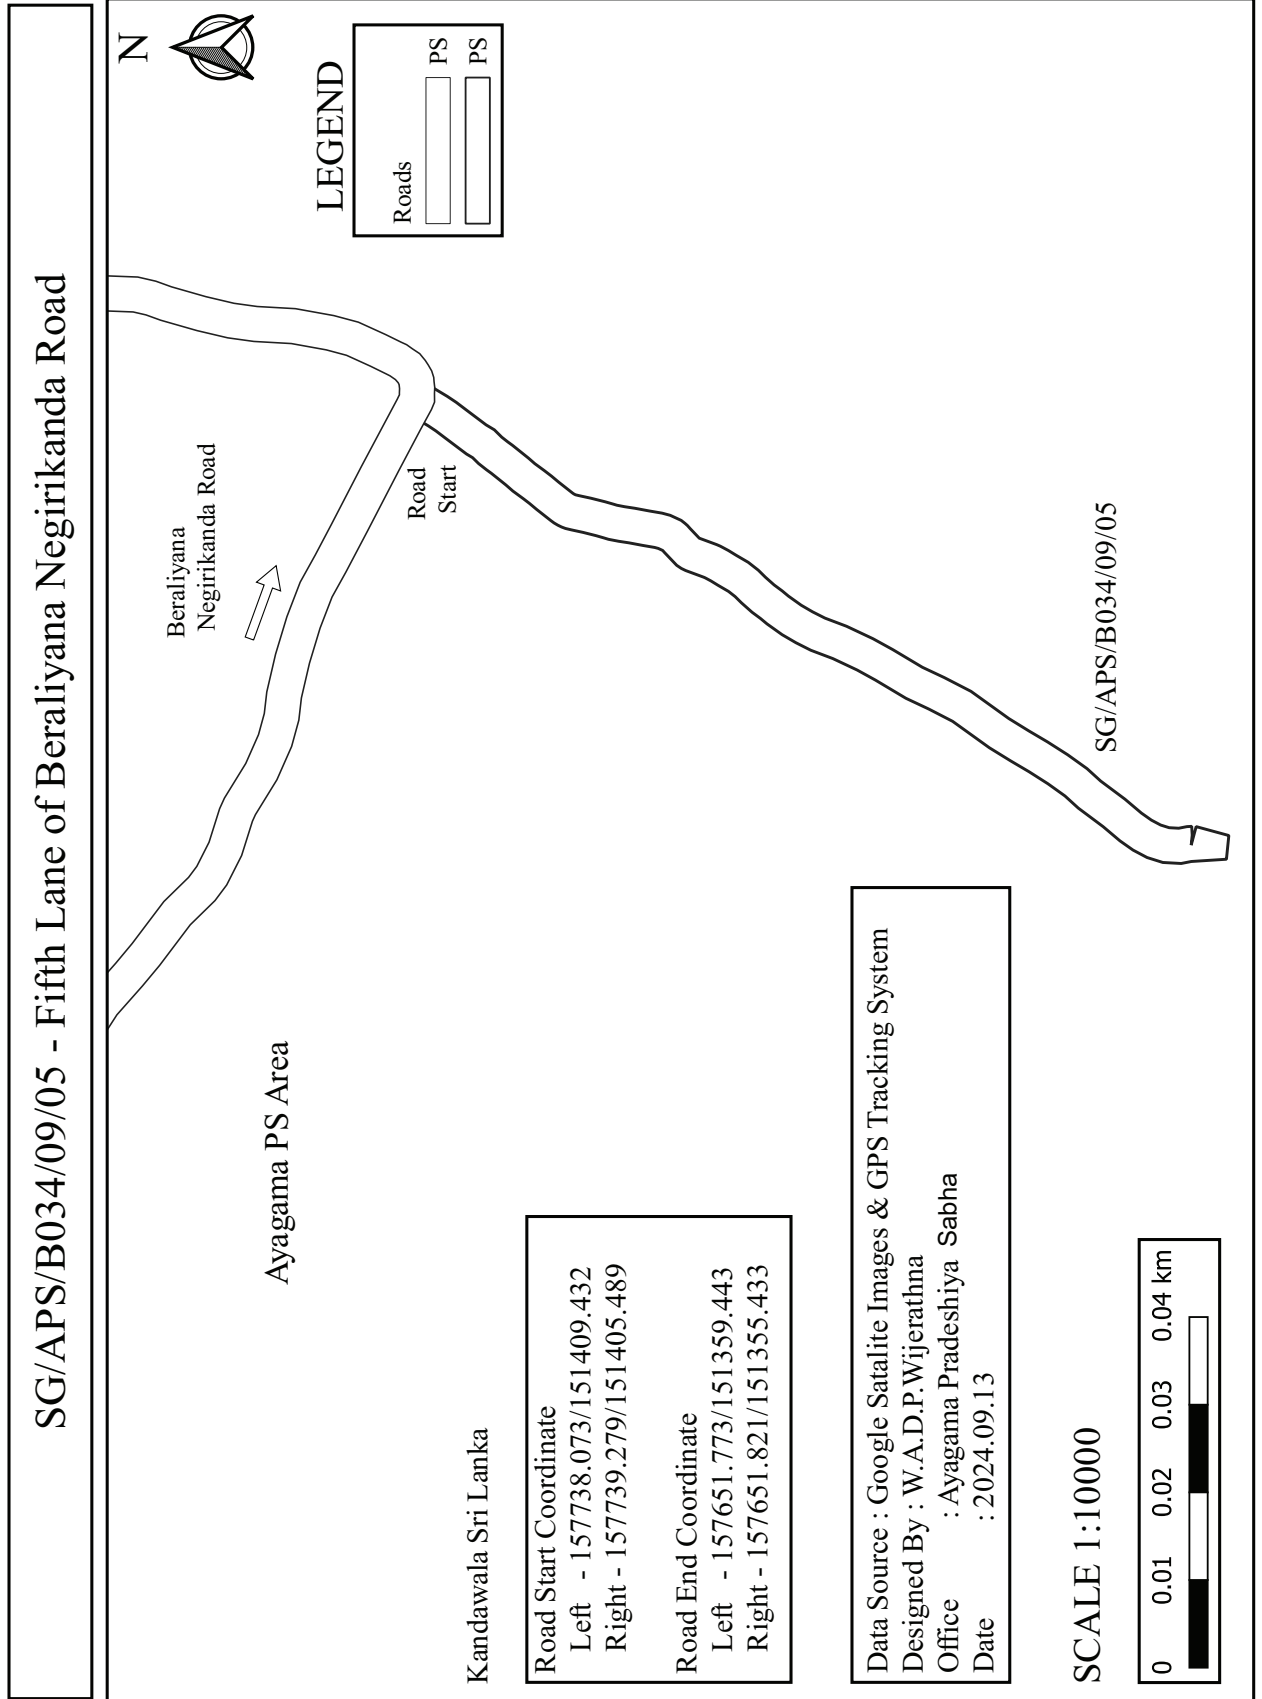


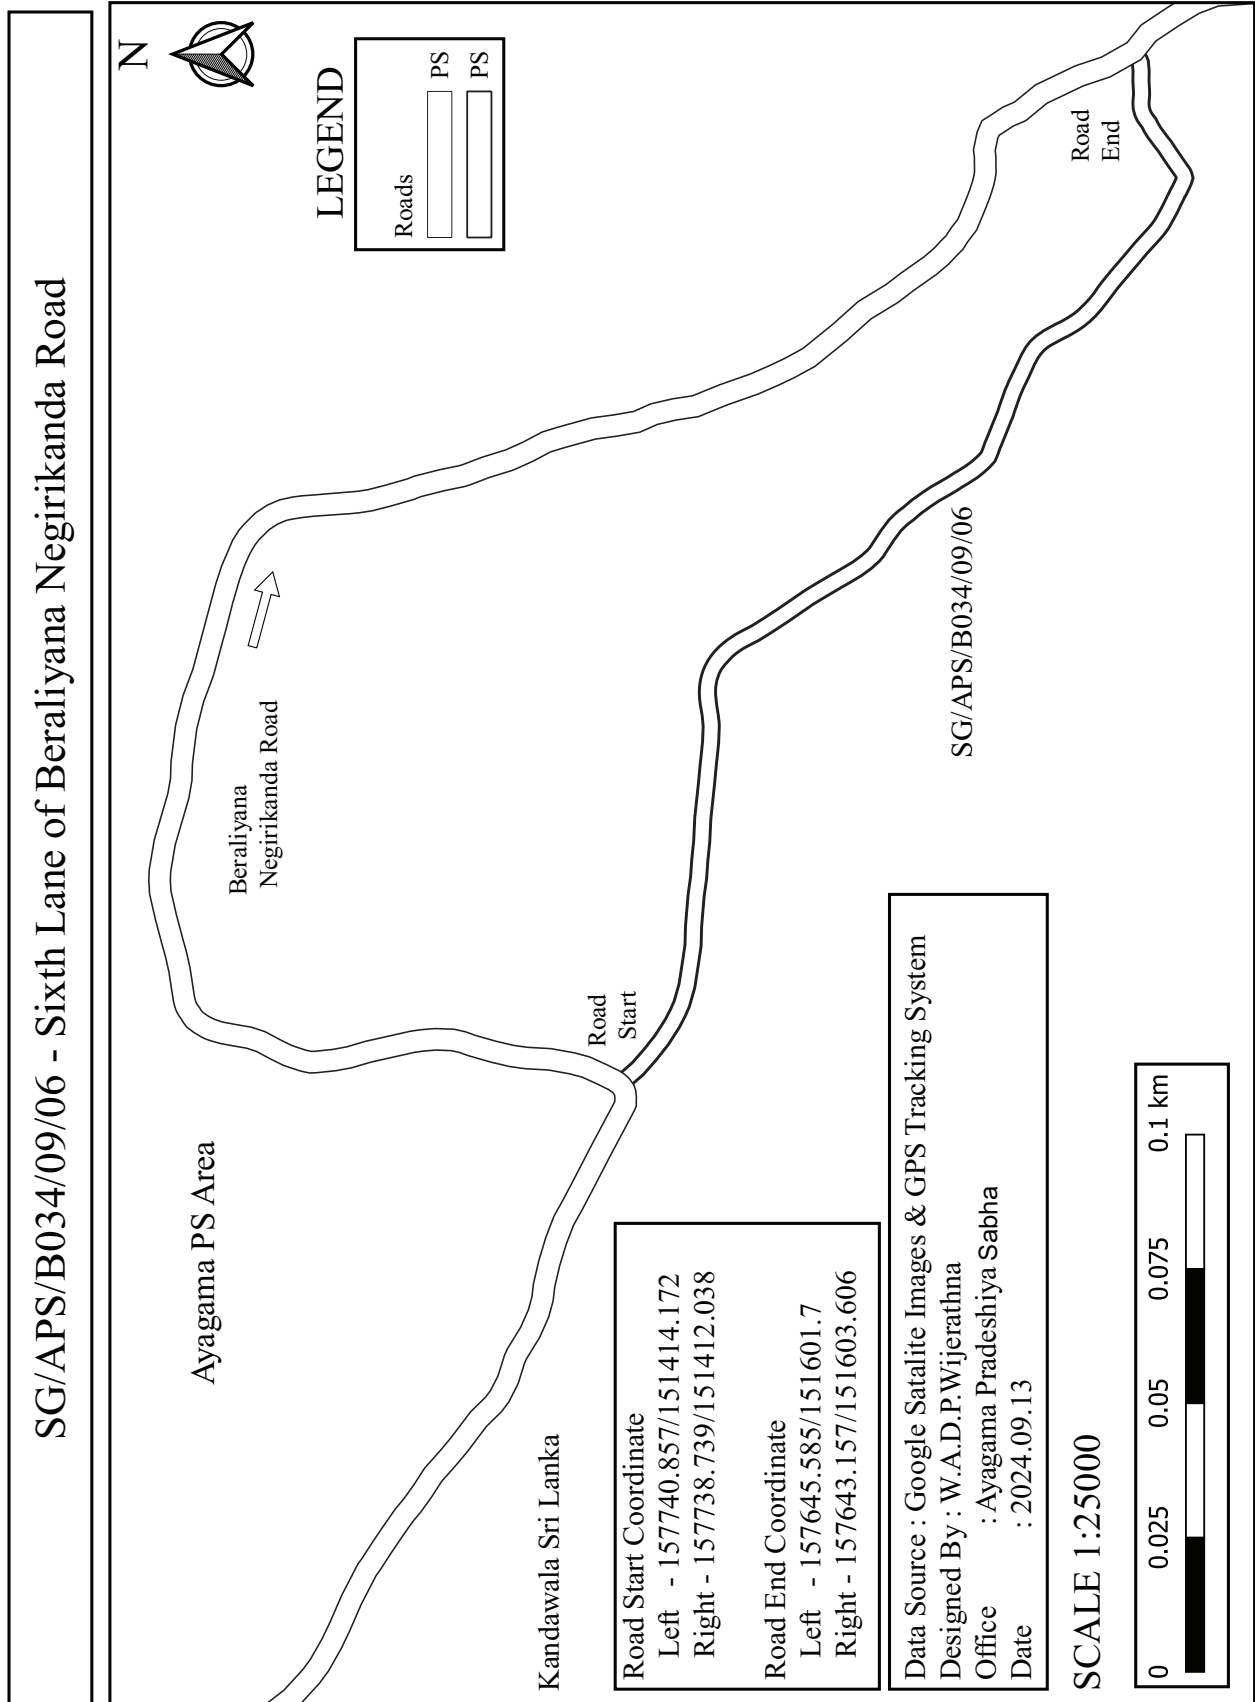


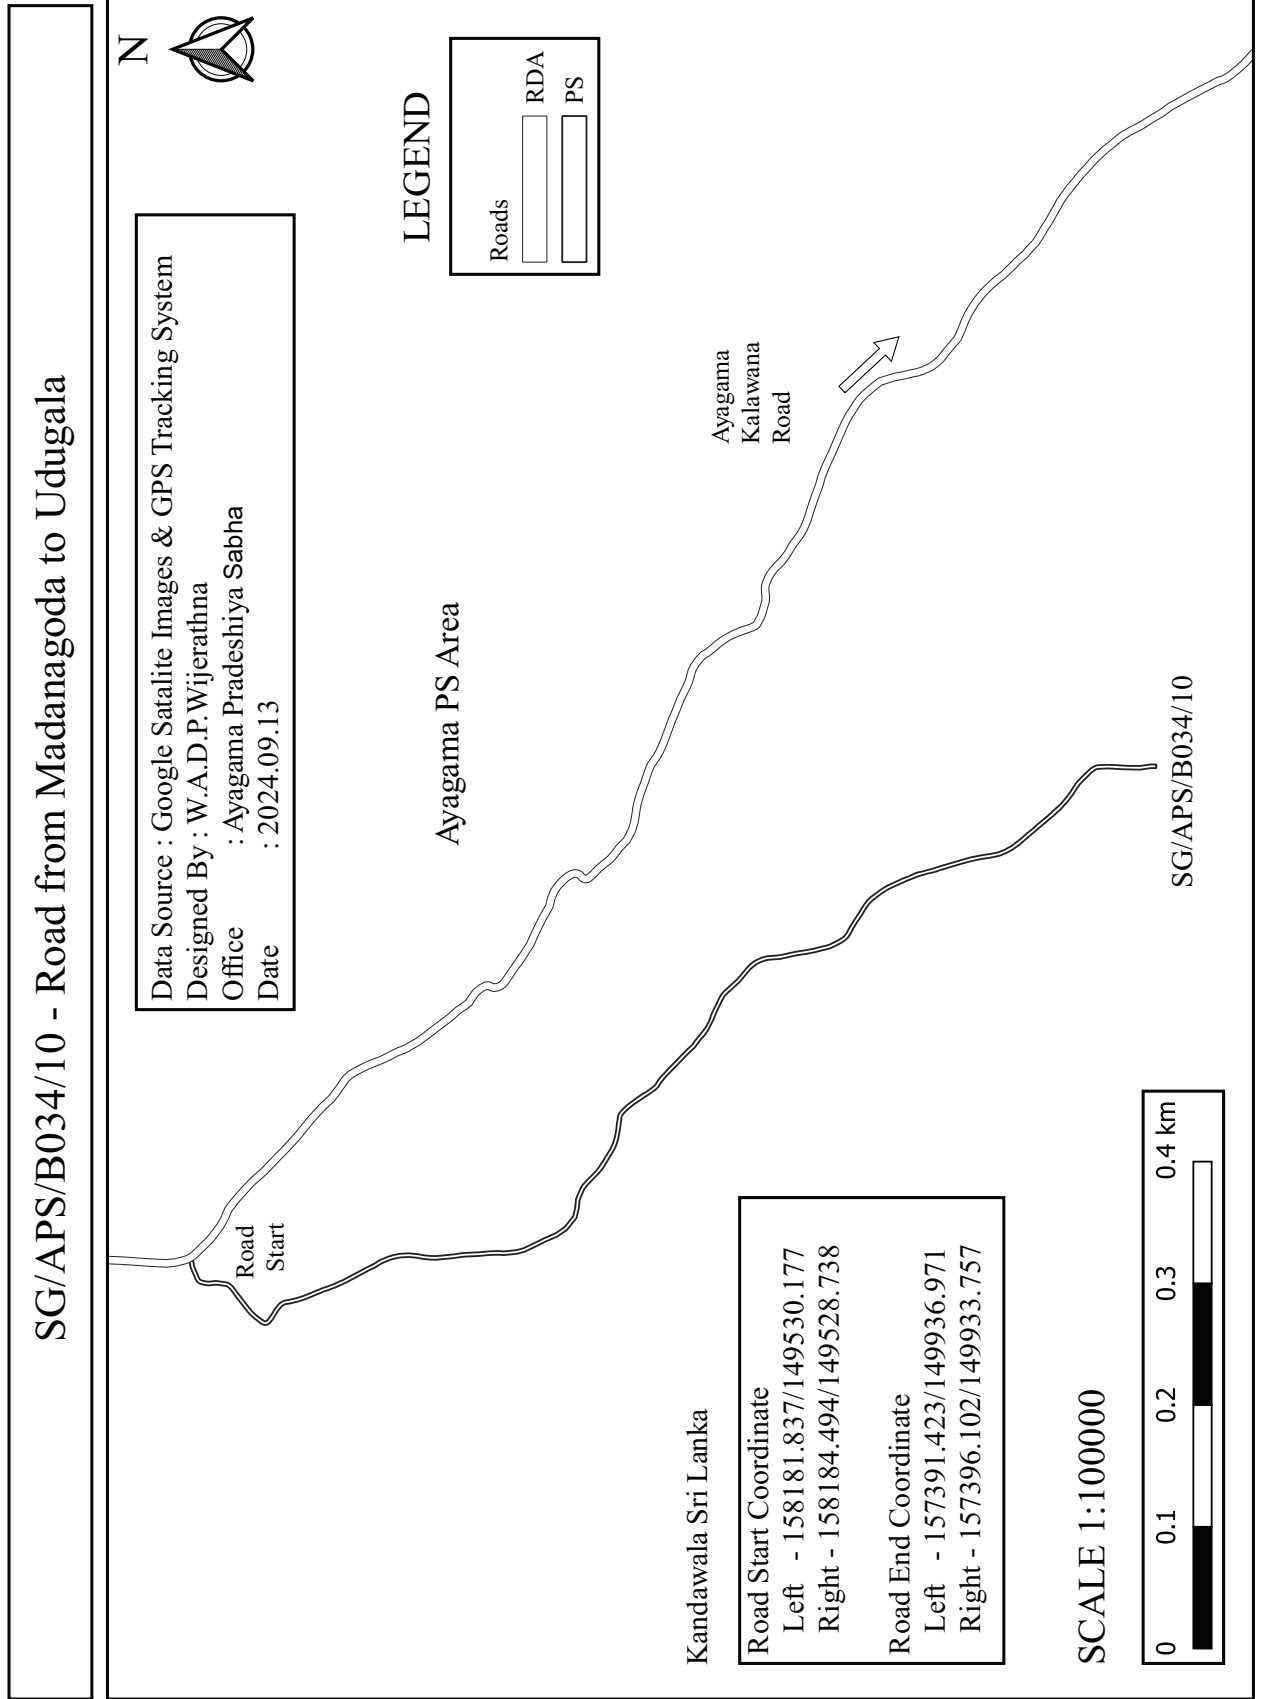


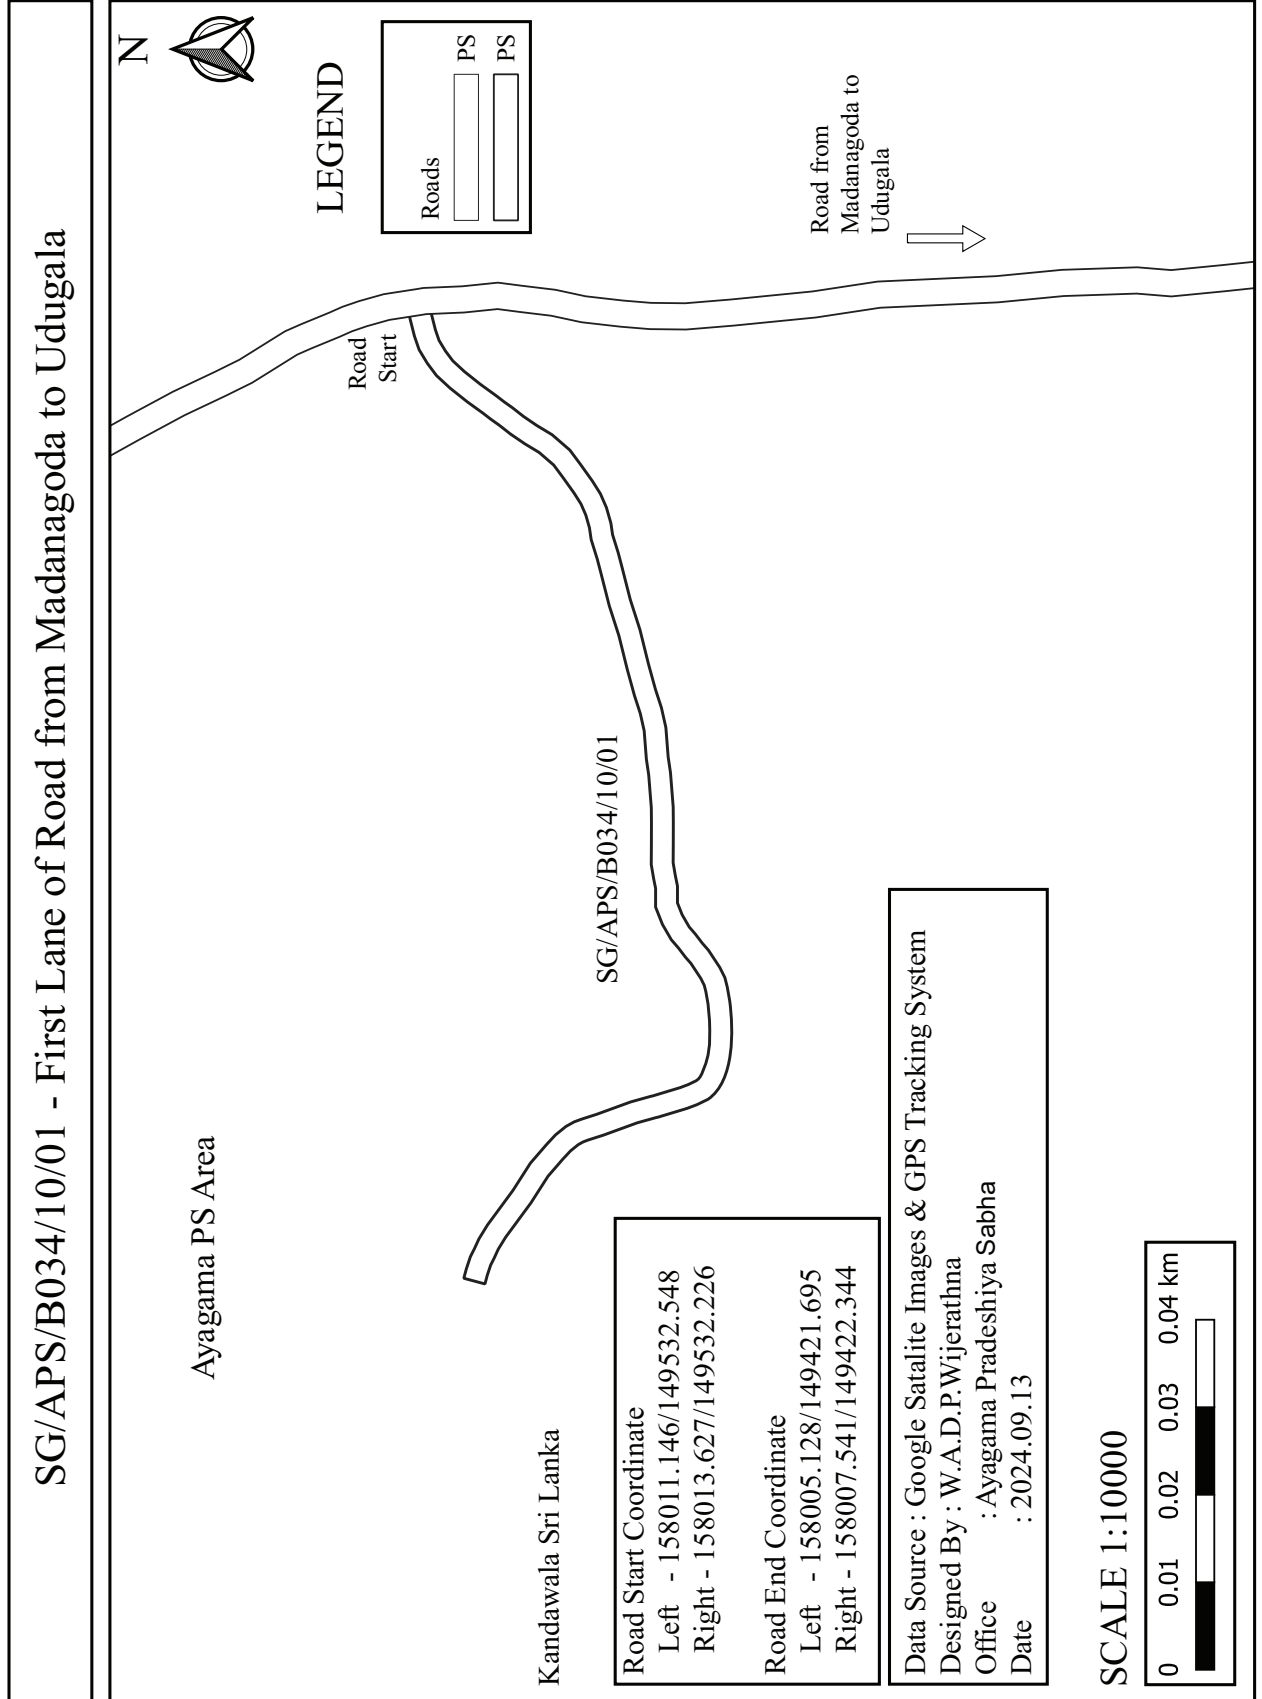


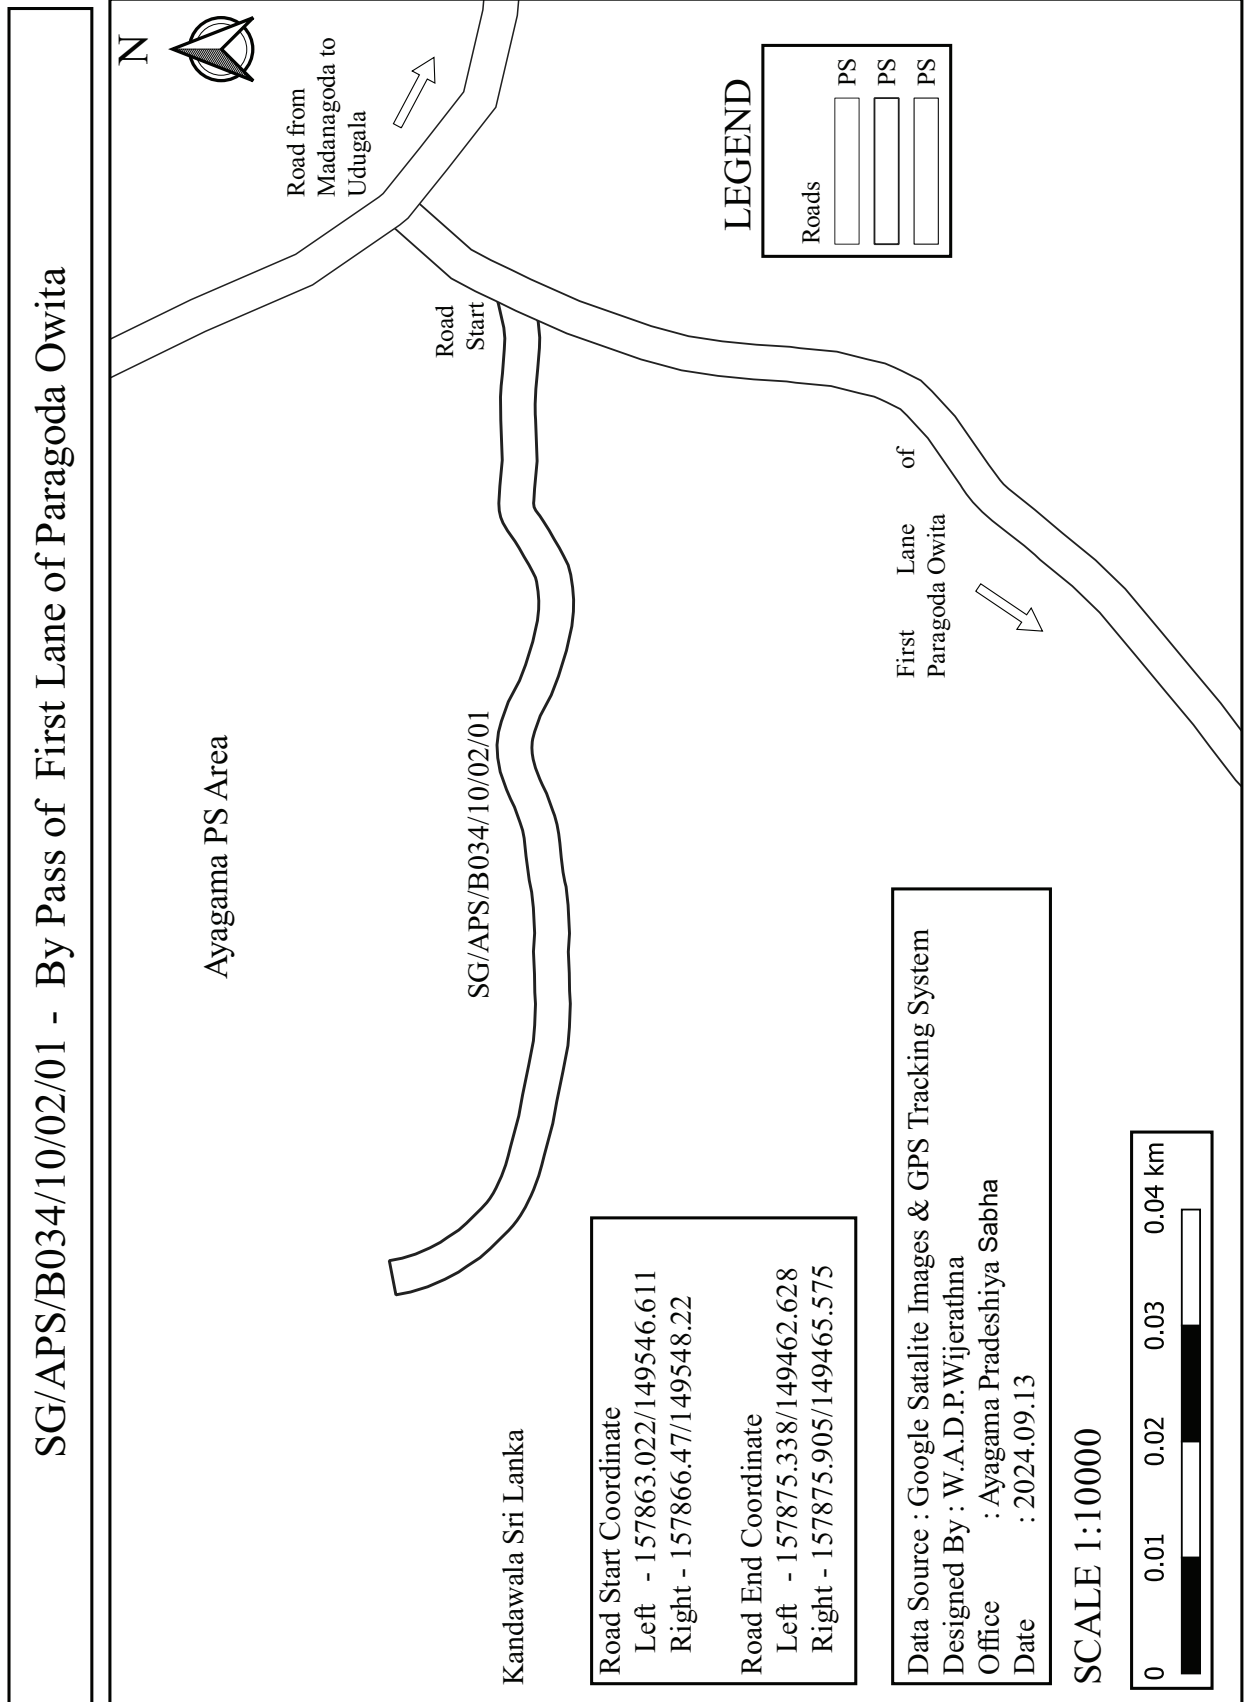


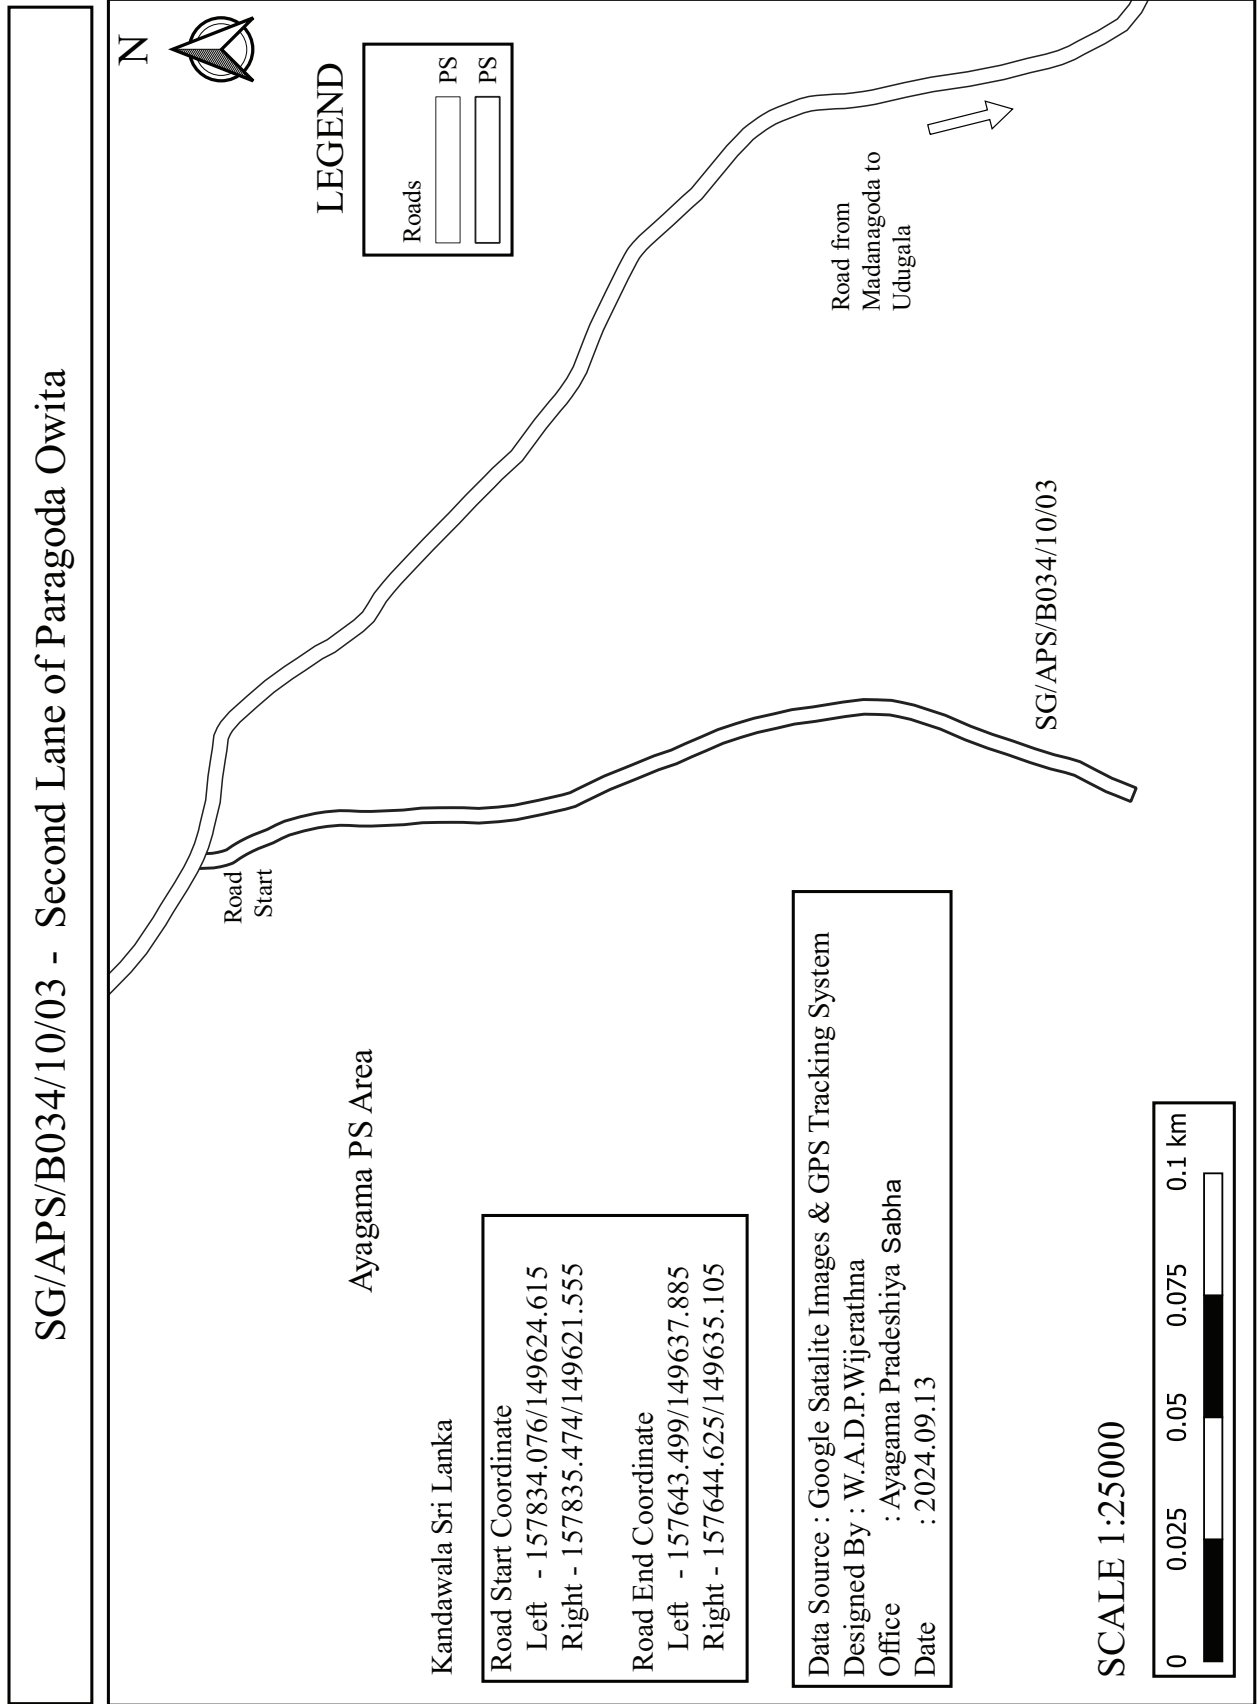


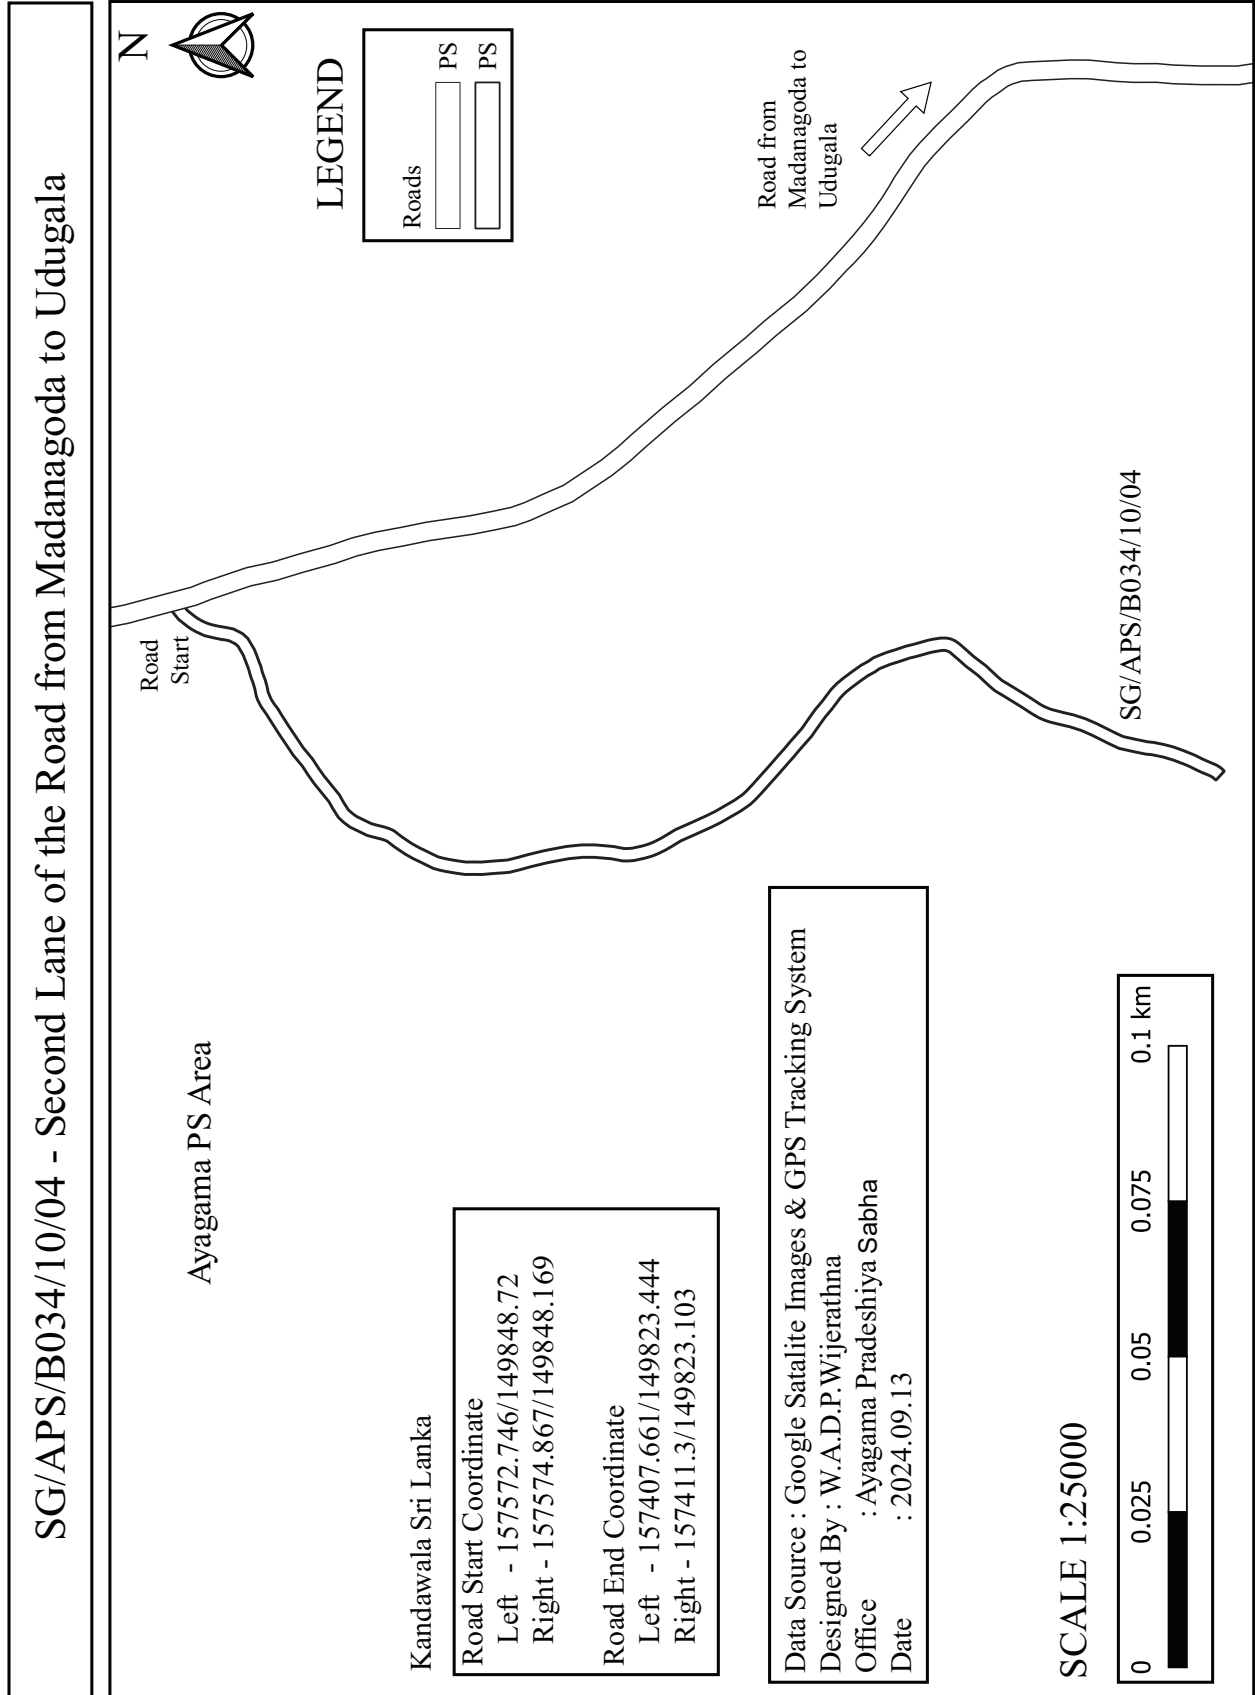


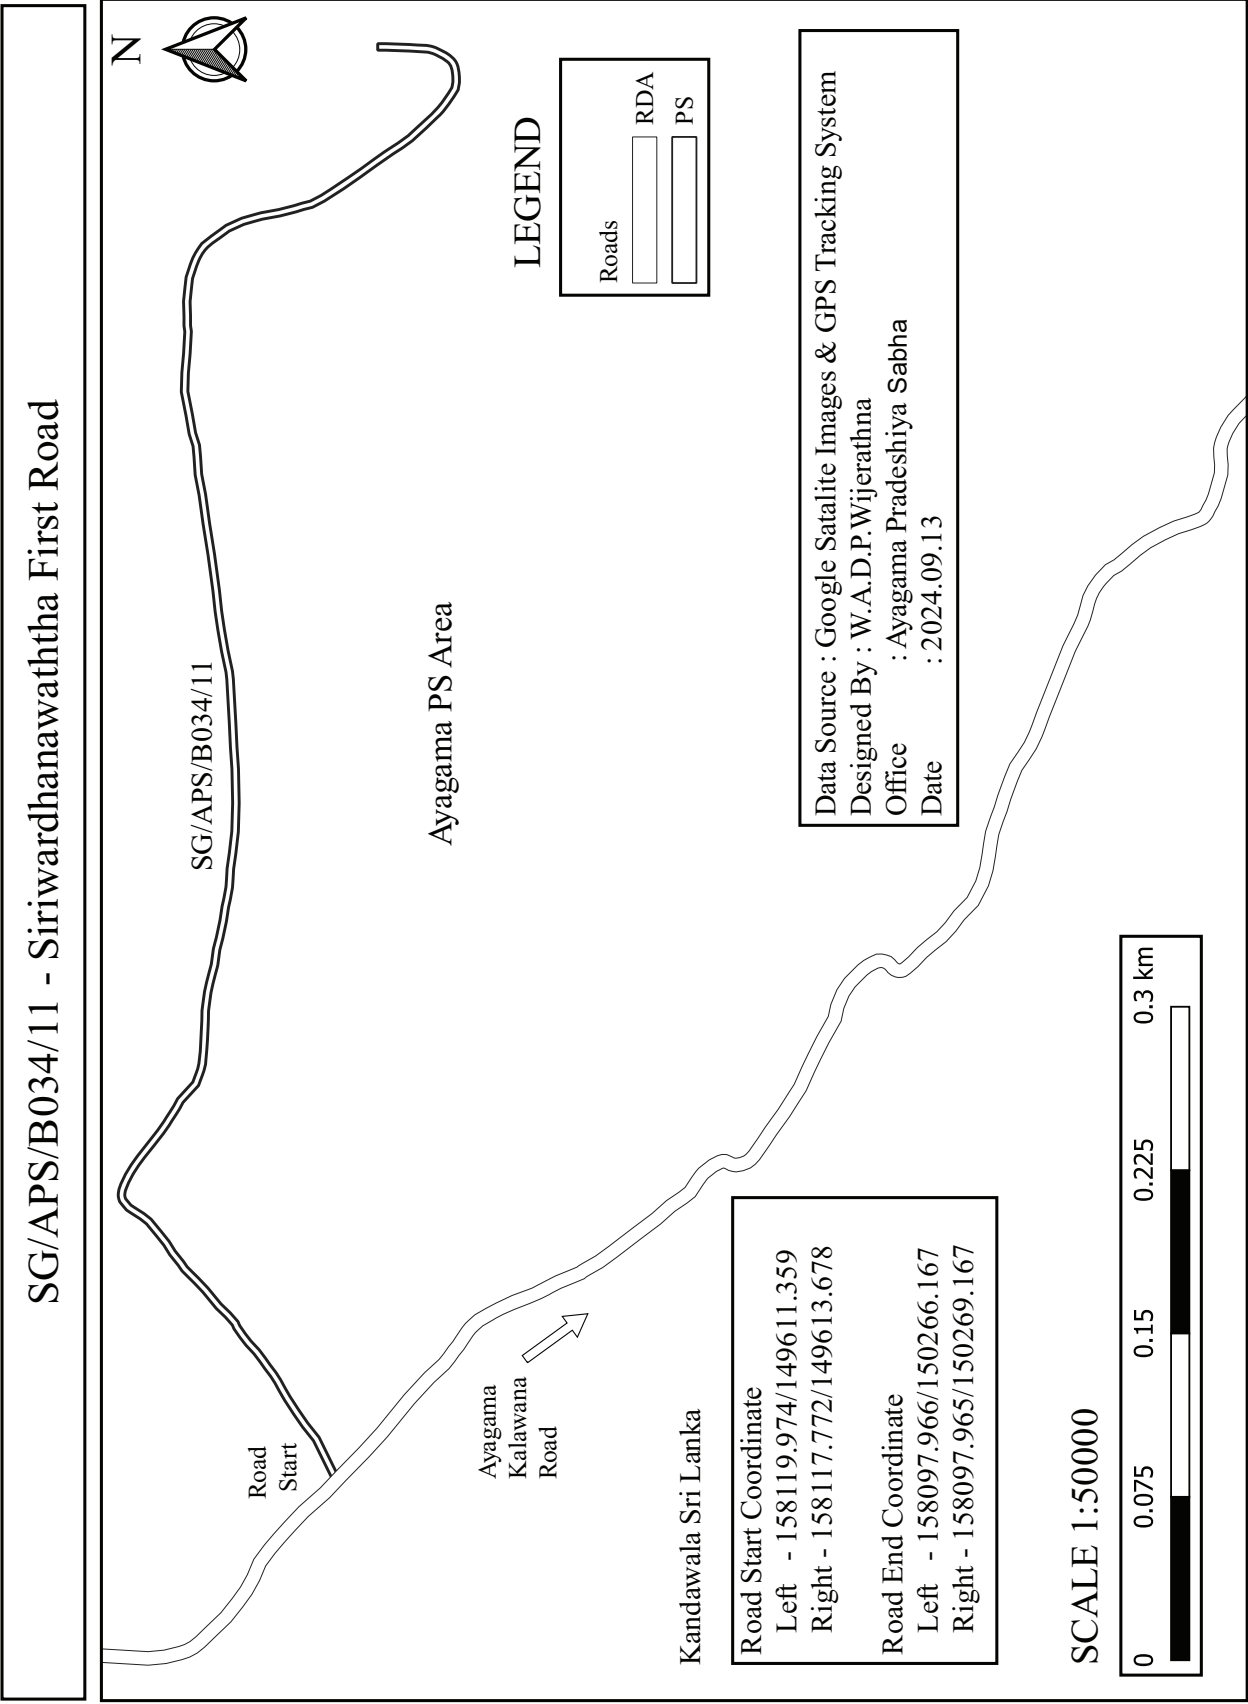


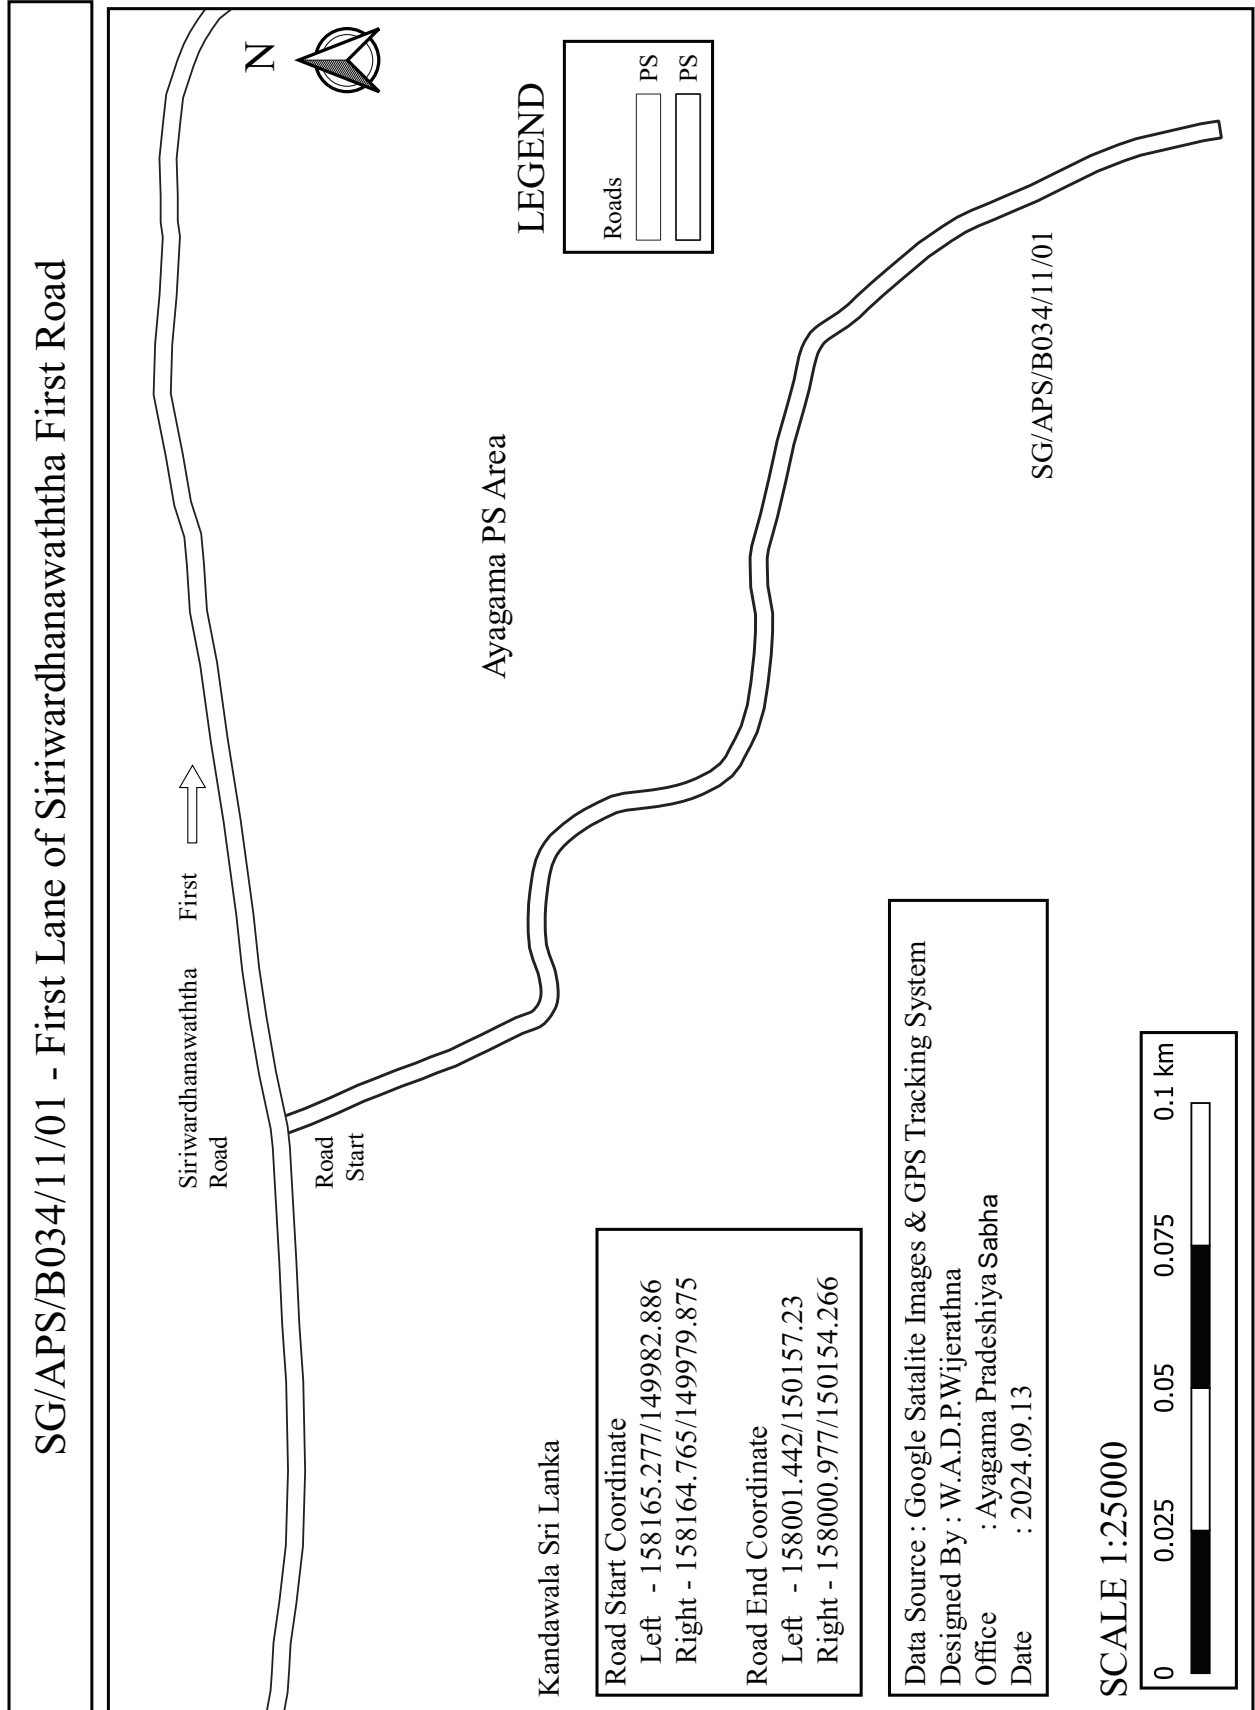


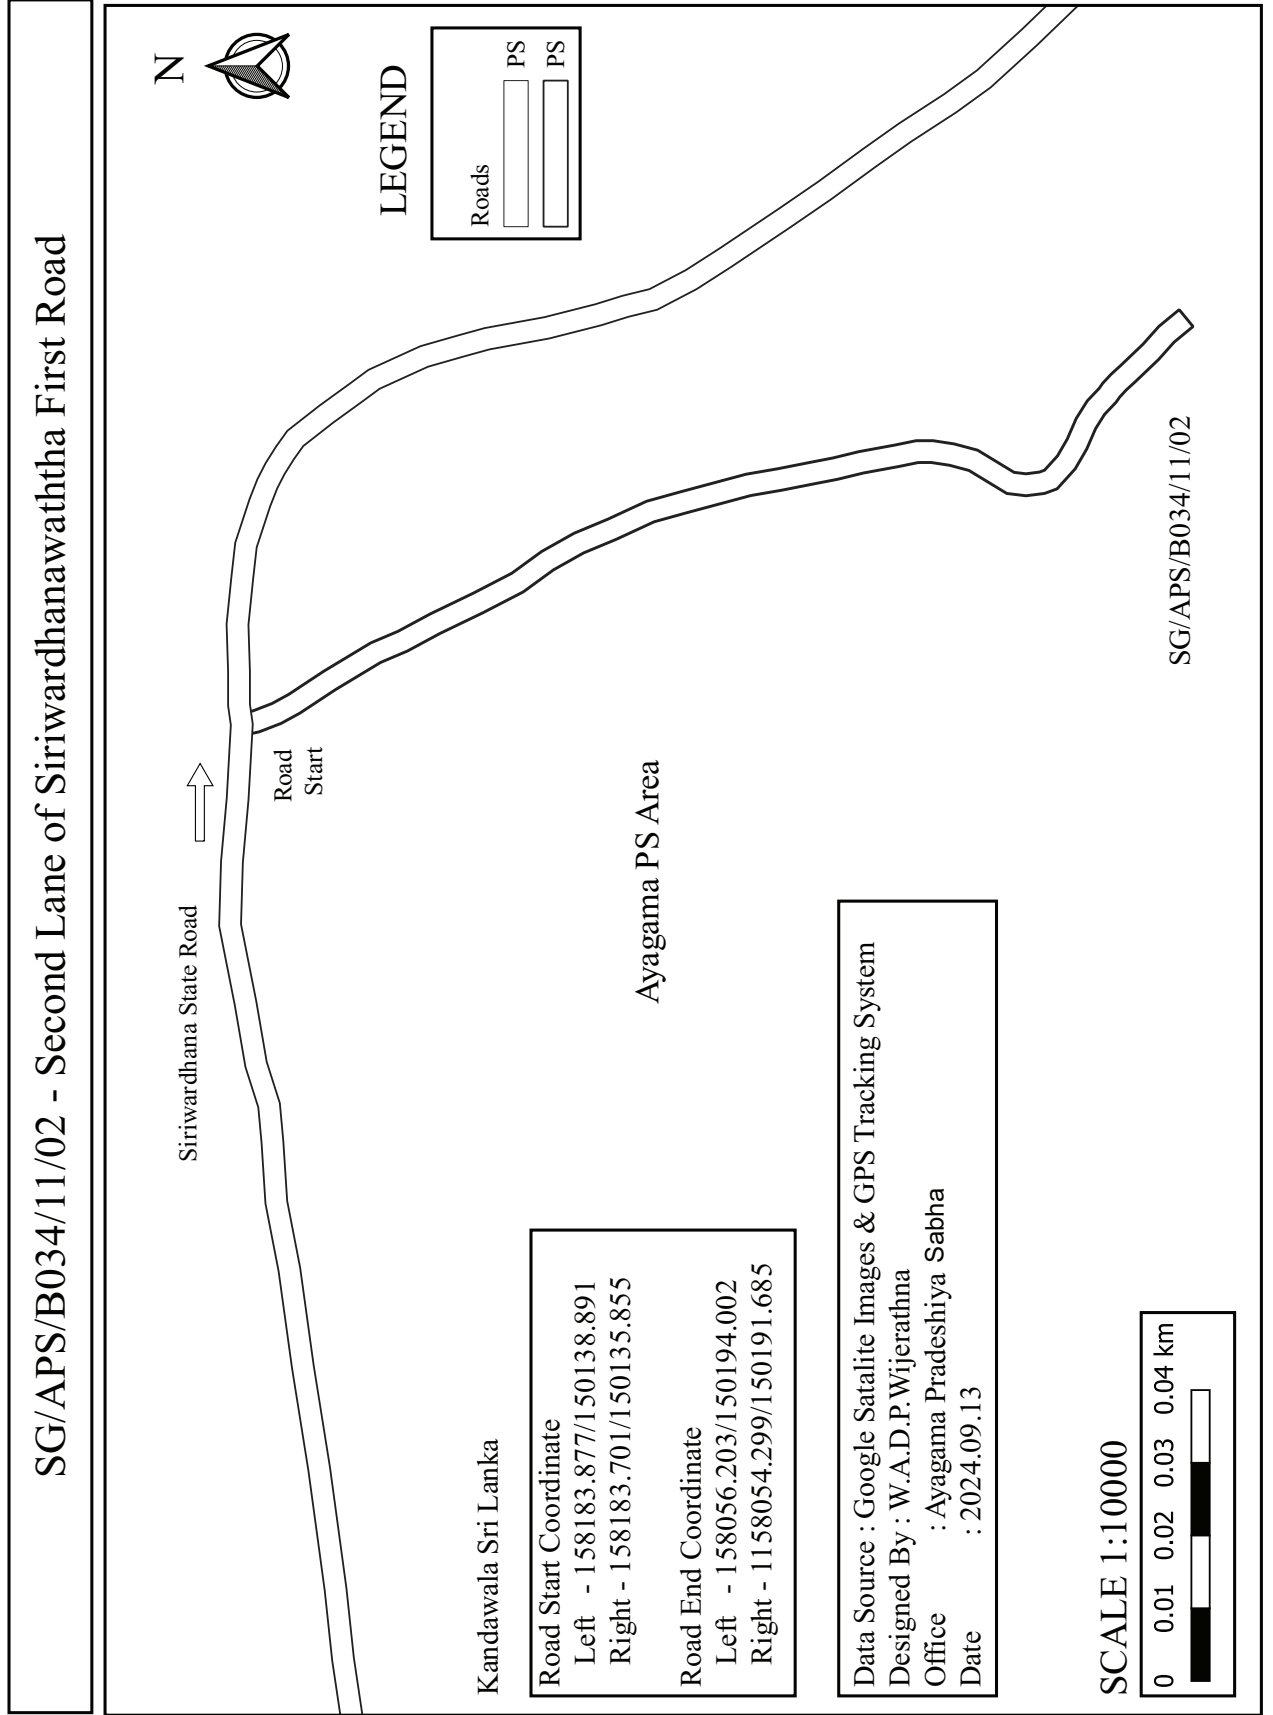


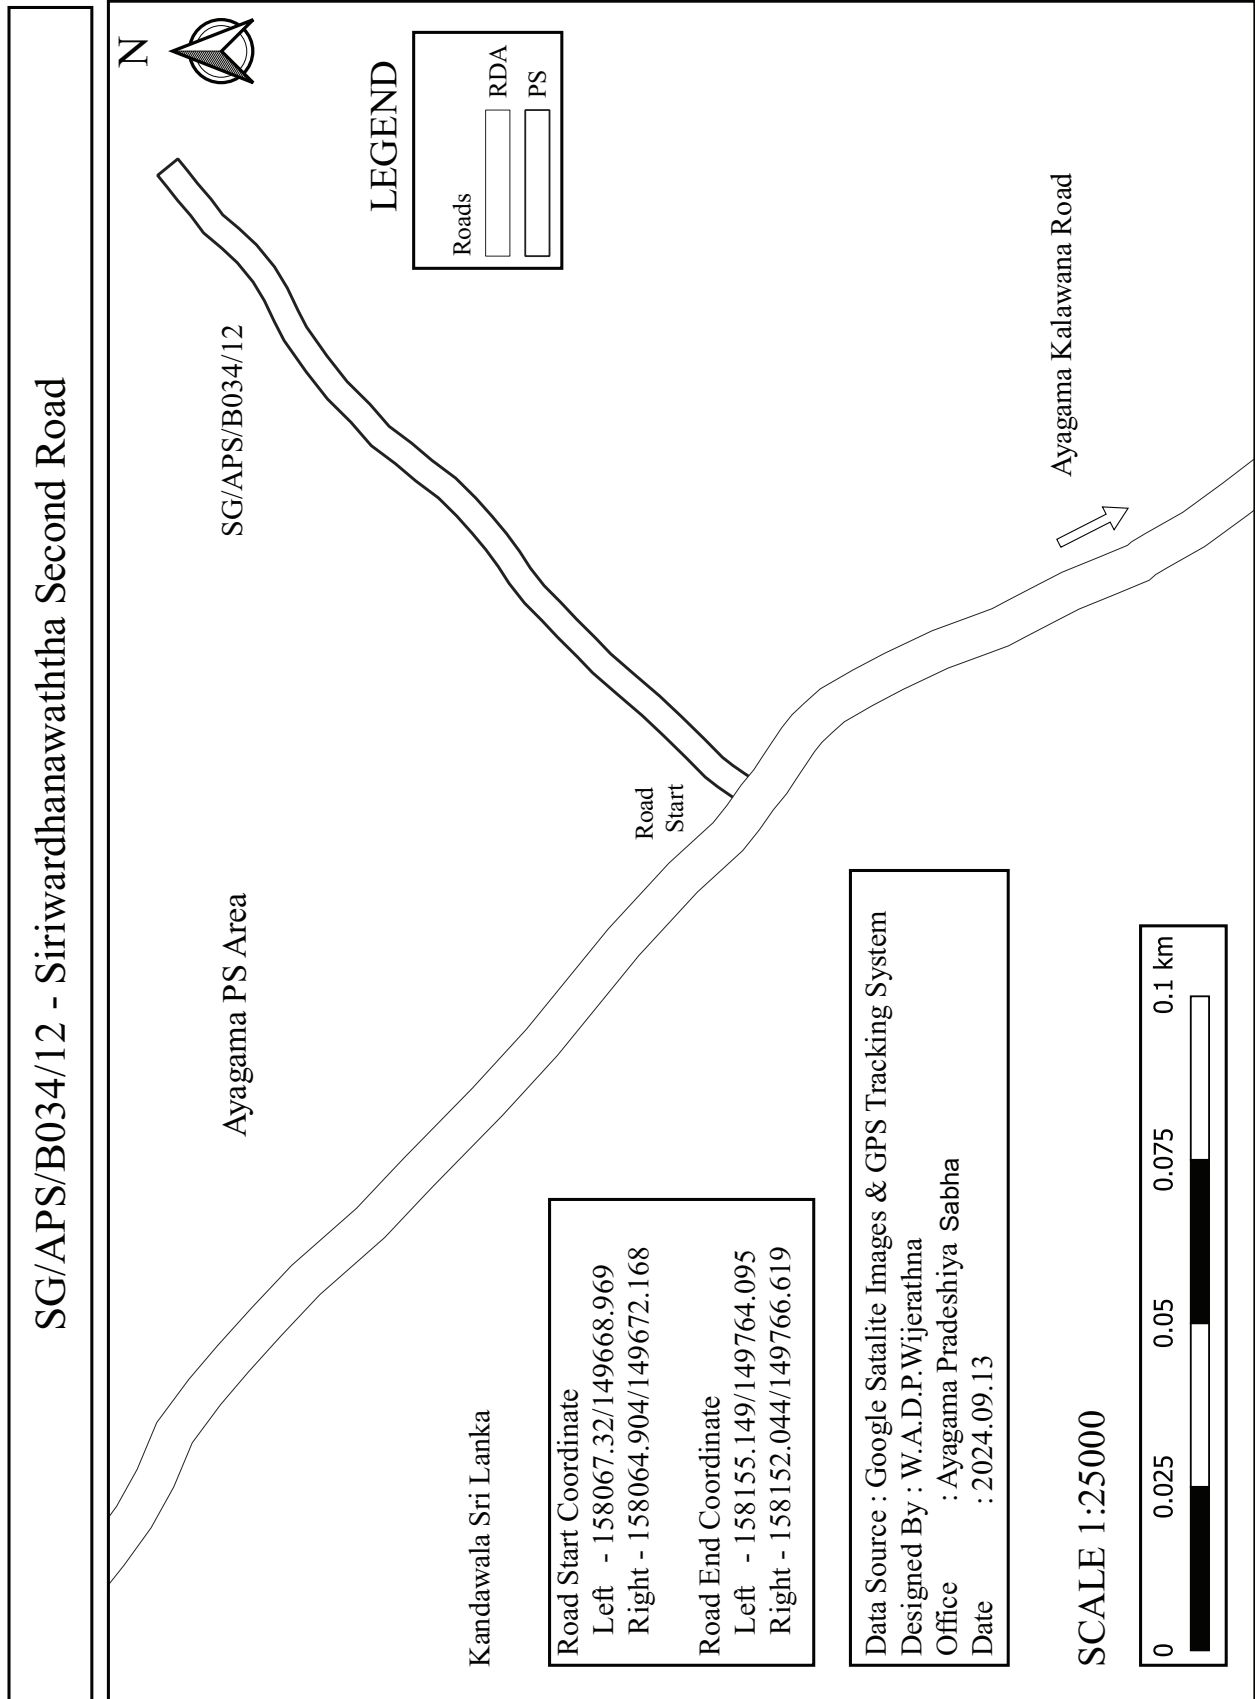

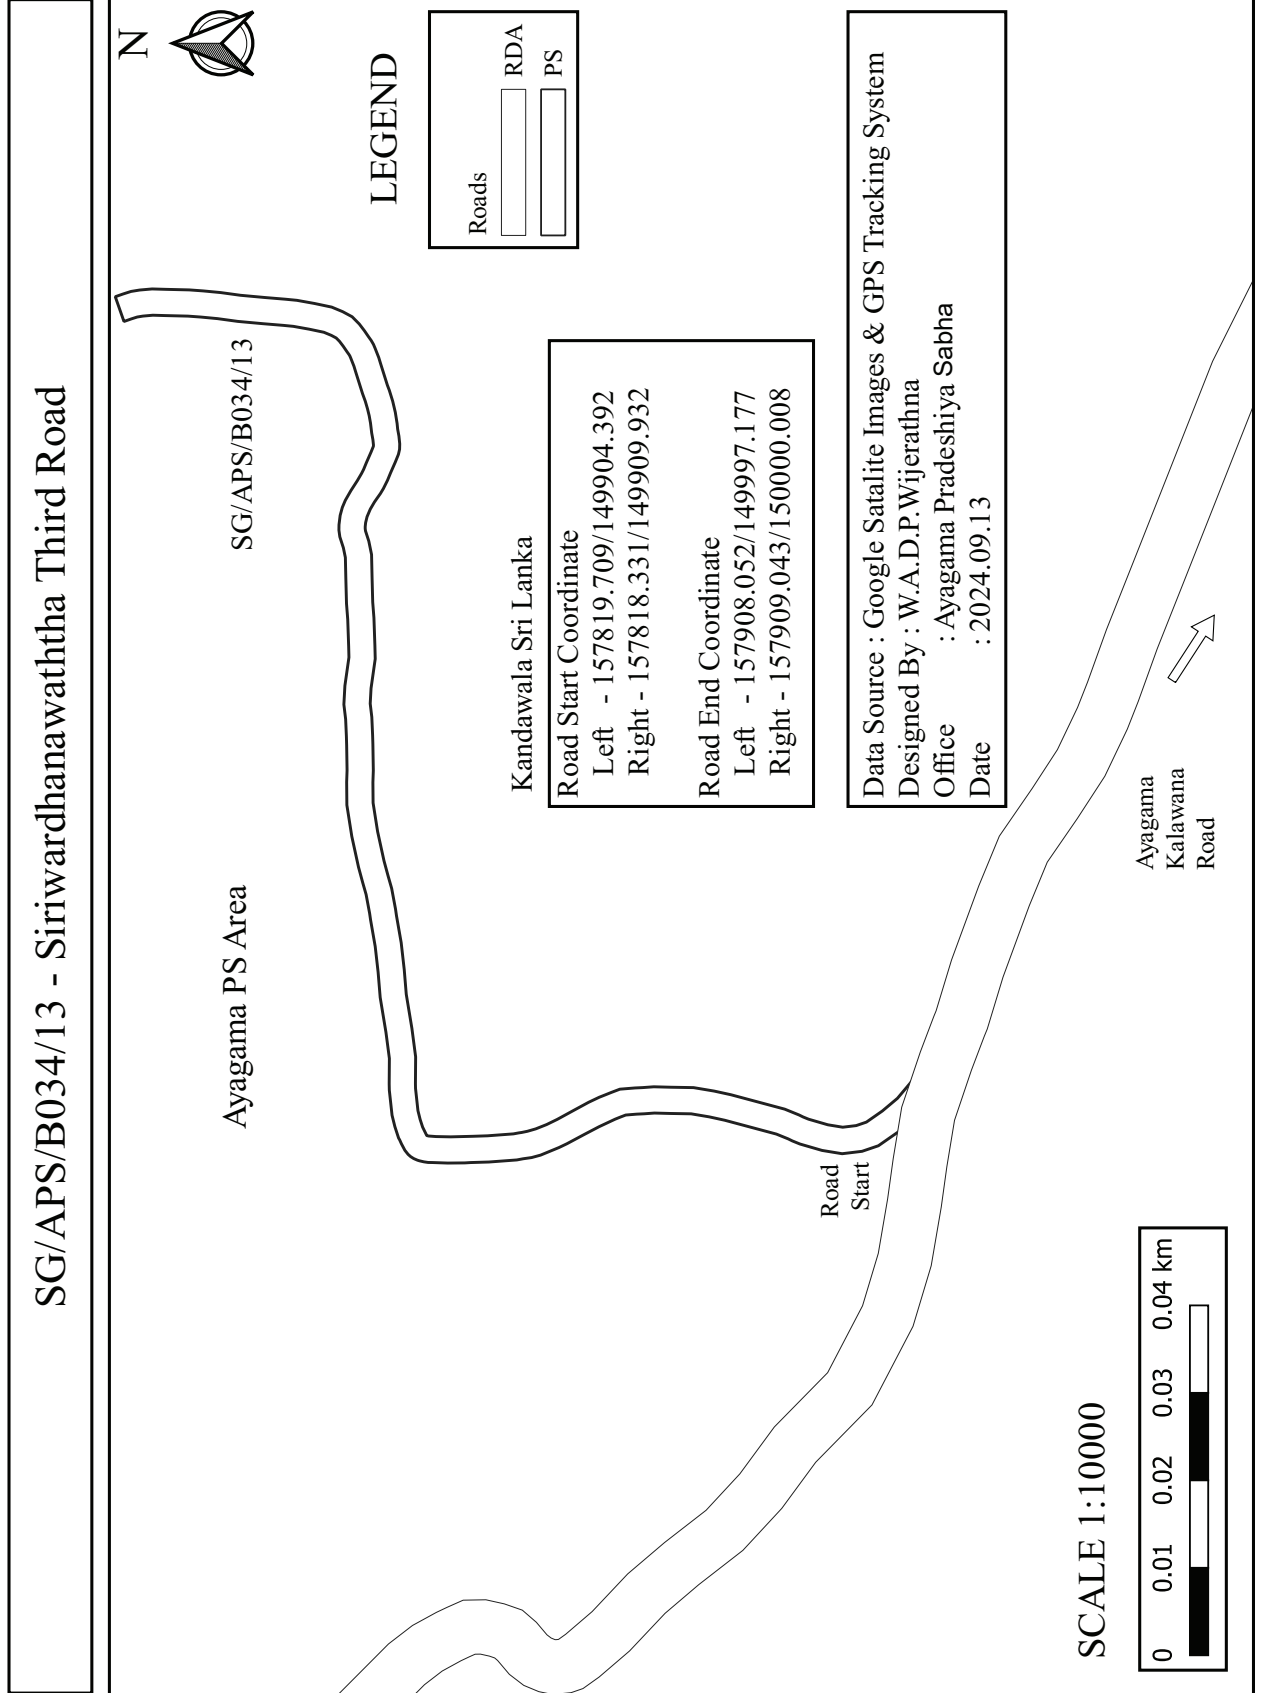

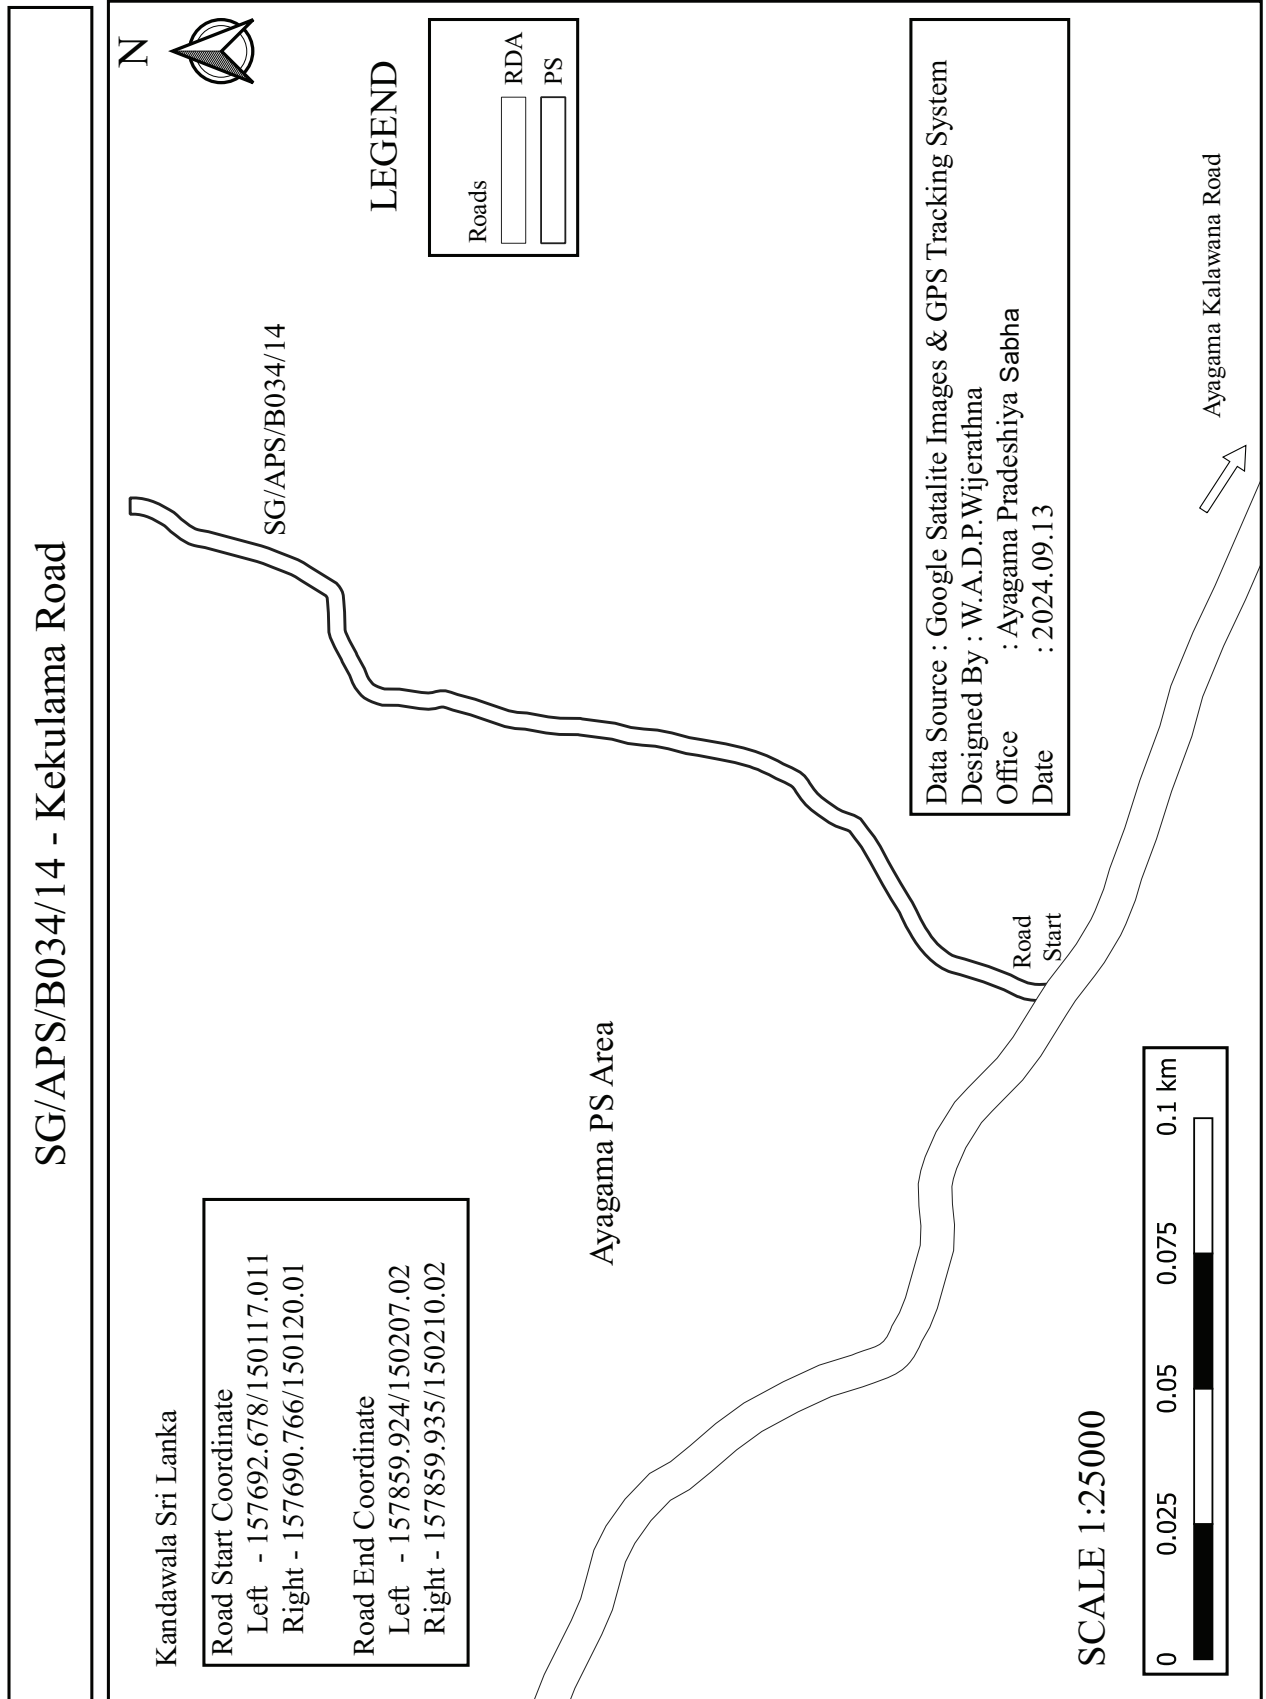

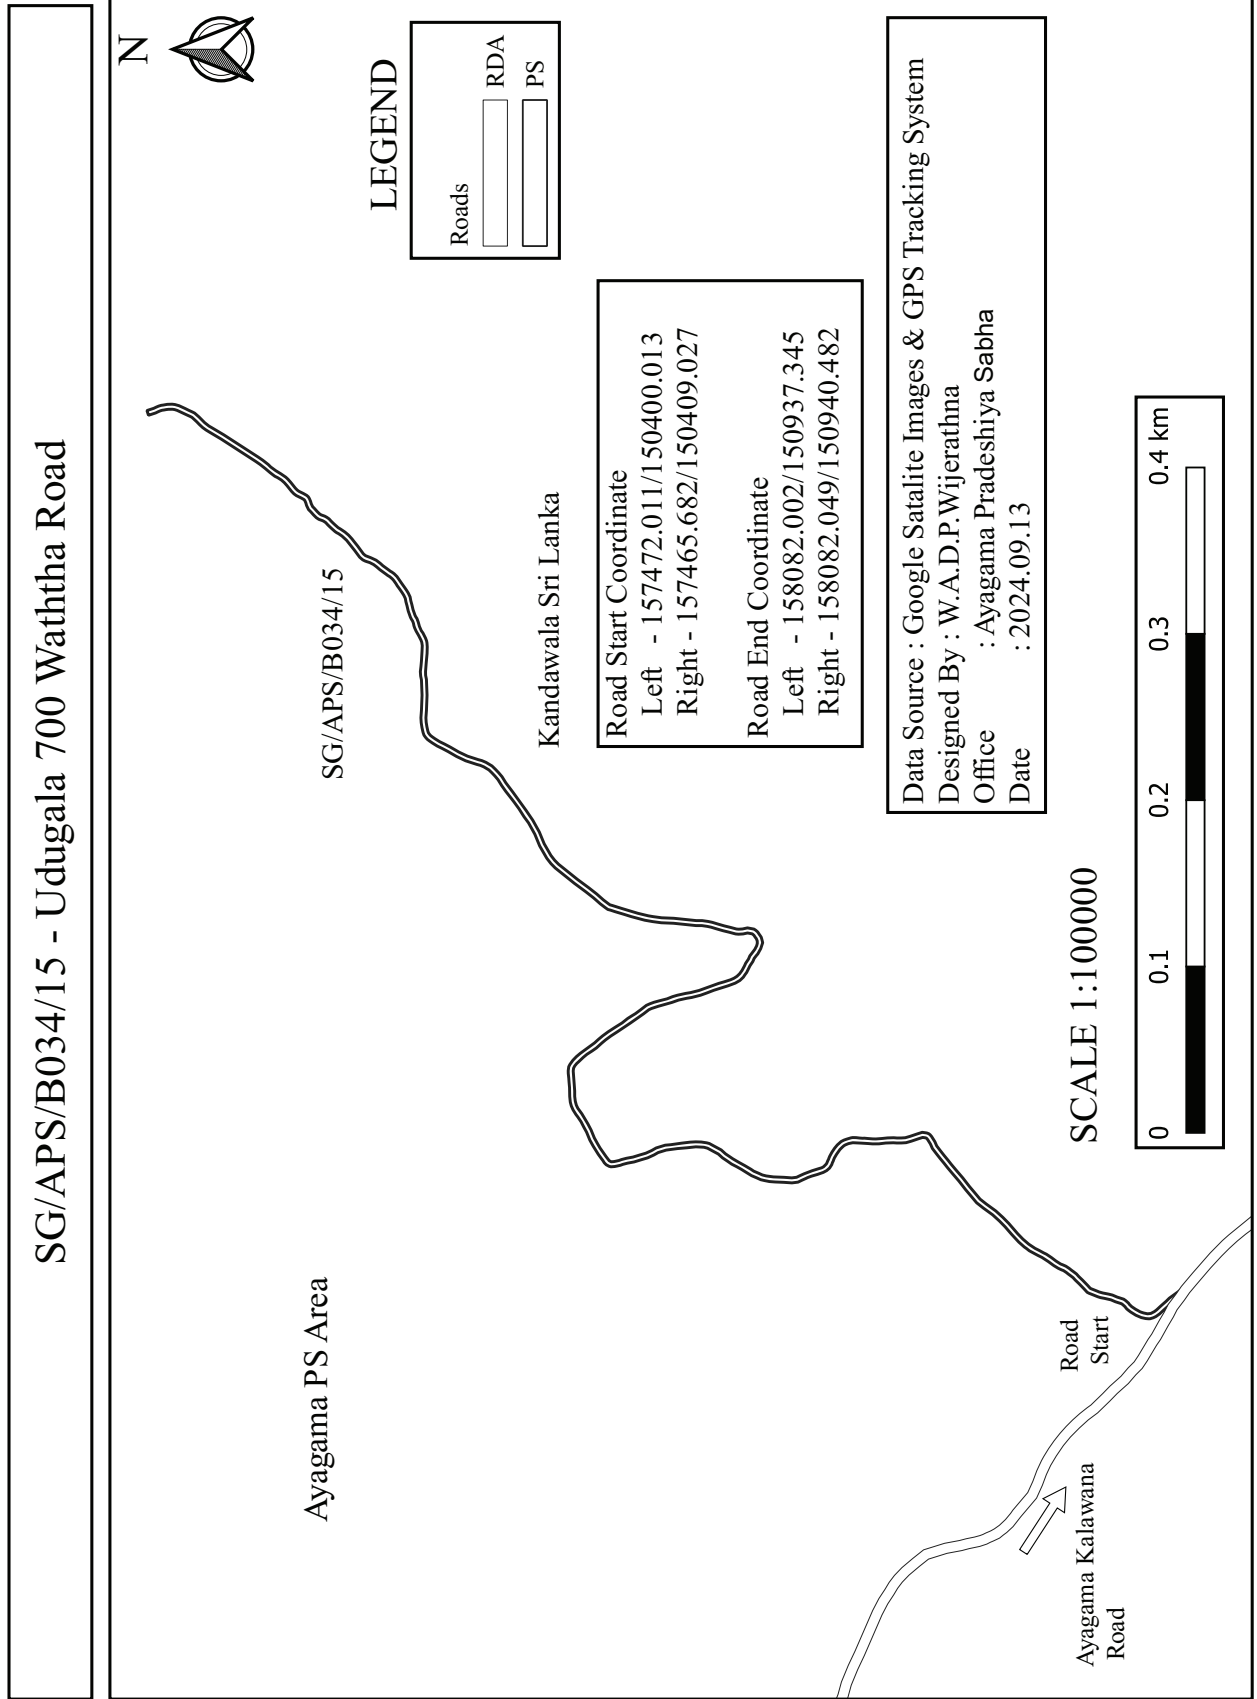

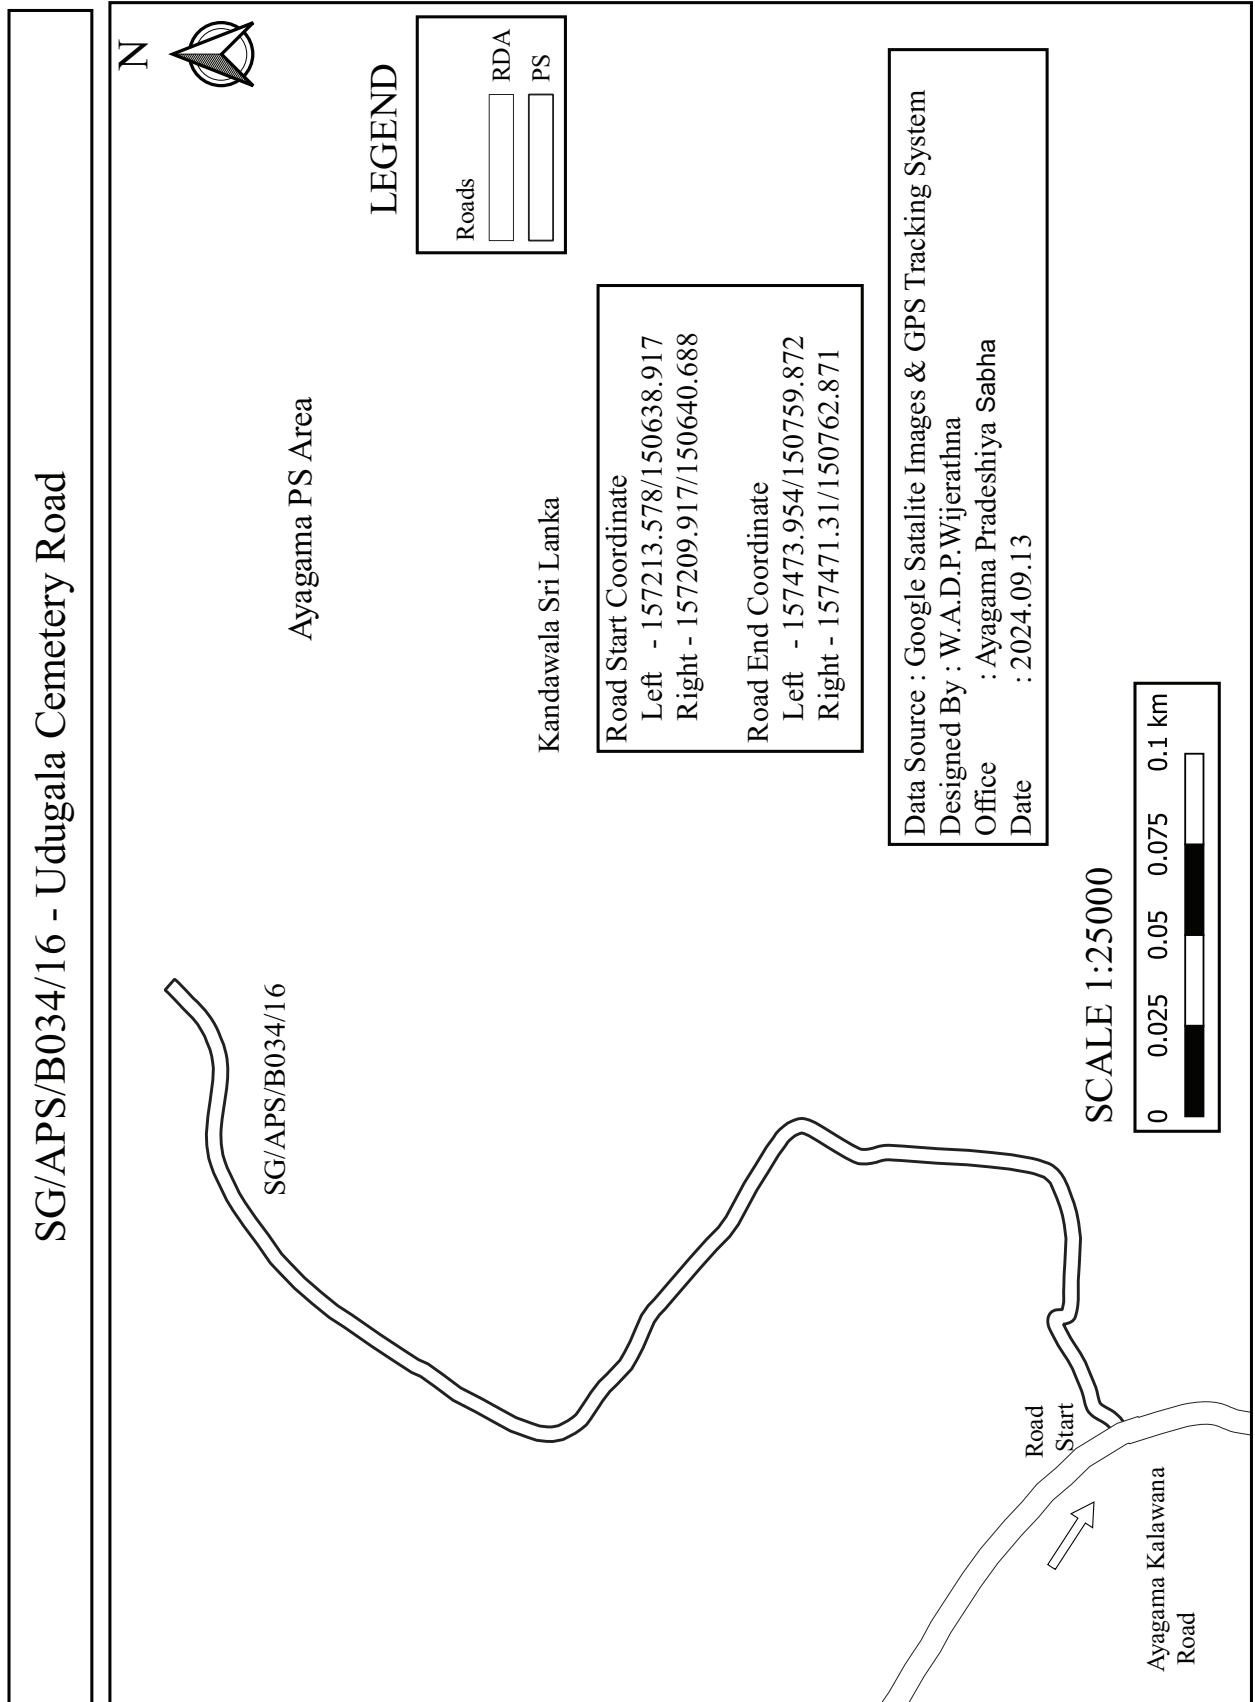

SG/APS/B034/16/01 - First Lane of Udagala Cemetery Road



LEGEND

Roads

PS

PS

SG/APS/B034/16/01

Ayagama PS Area

Udagala Cemetery Road

Road
Start

Kandawala Sri Lanka

Road Start Coordinate

Left - 157441.317/150680.703

Right - 157443.508/150682.996

Road End Coordinate

Left - 157490.669/150671.598

Right - 157491.717/150674.145

SCALE 1:10000


0 0.01 0.02 0.03 0.04 km


Data Source : Google Satalite Images & GPS Tracking System


Designed By : W.A.D.P.Wijerathna


Office : Ayagama Pradeshiya Sabha


Date : 2024.09.13

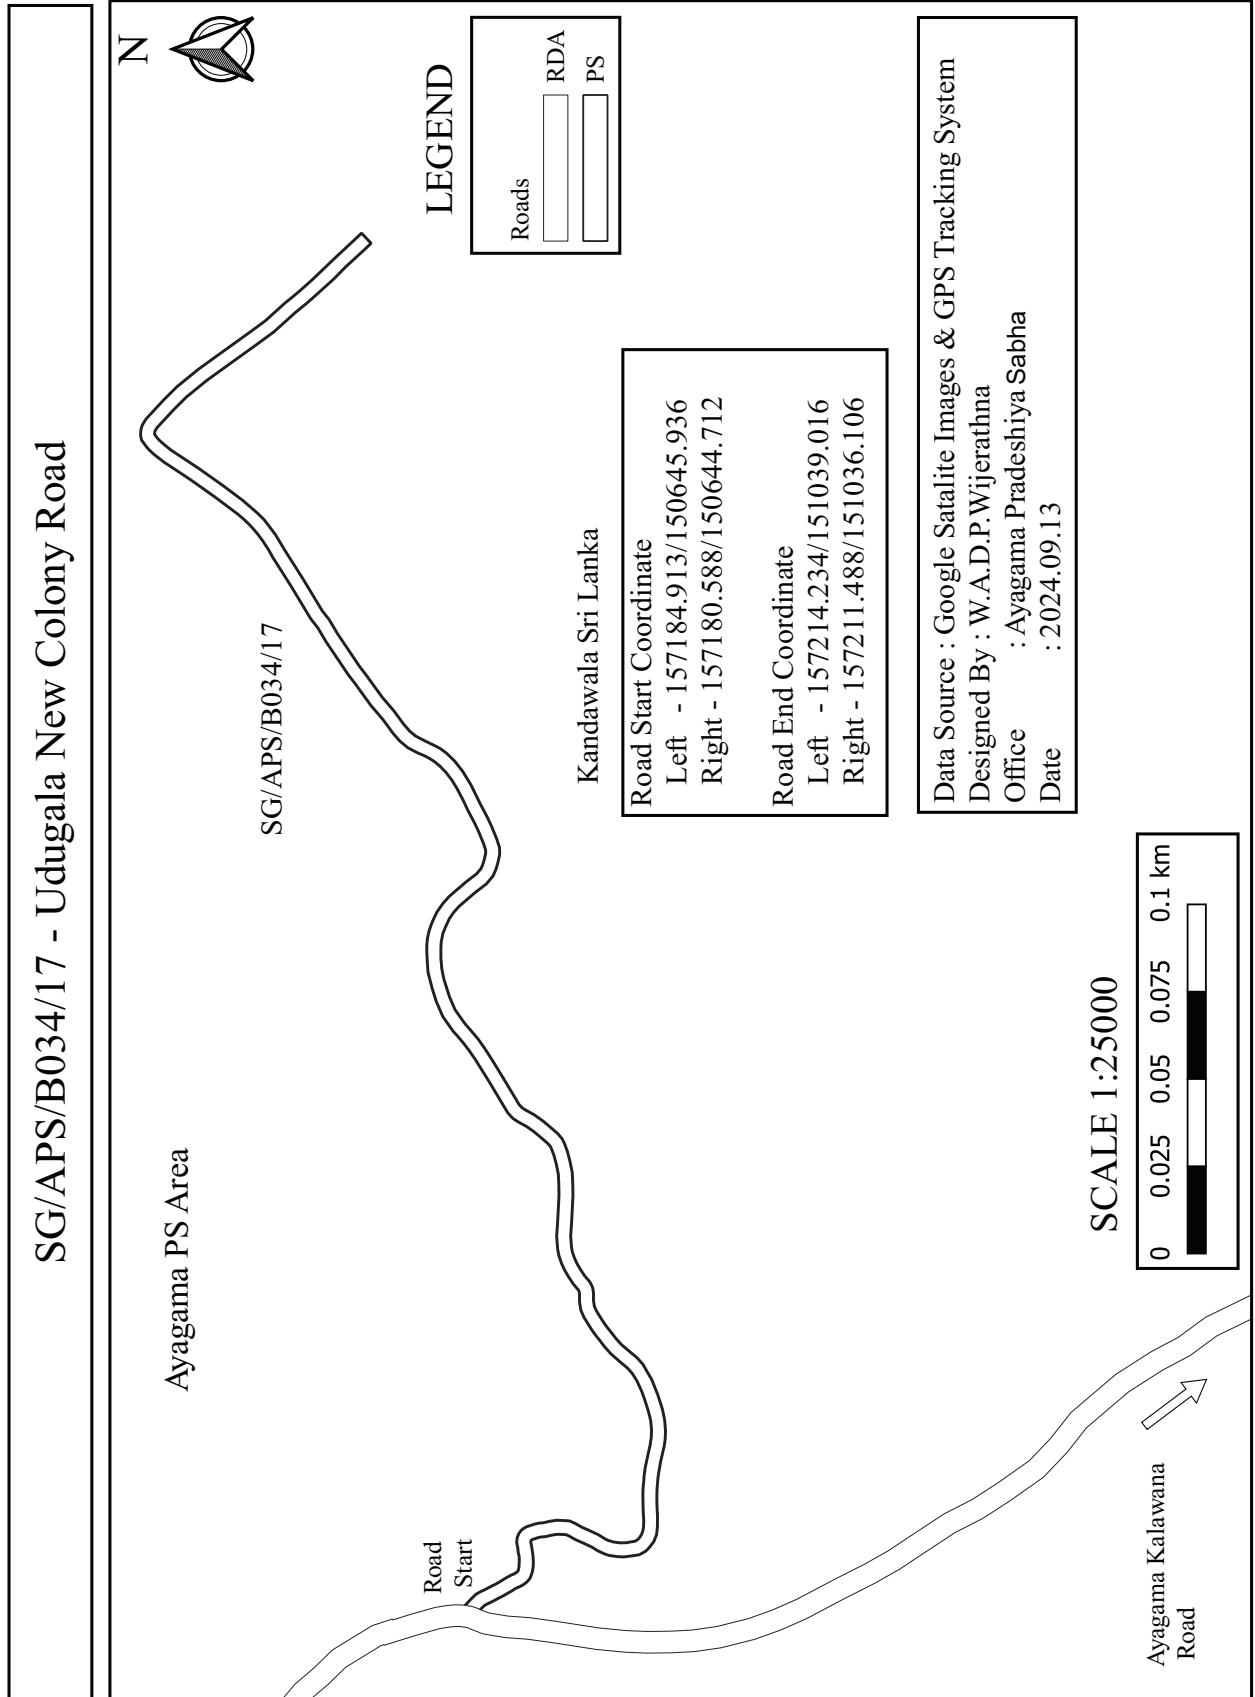


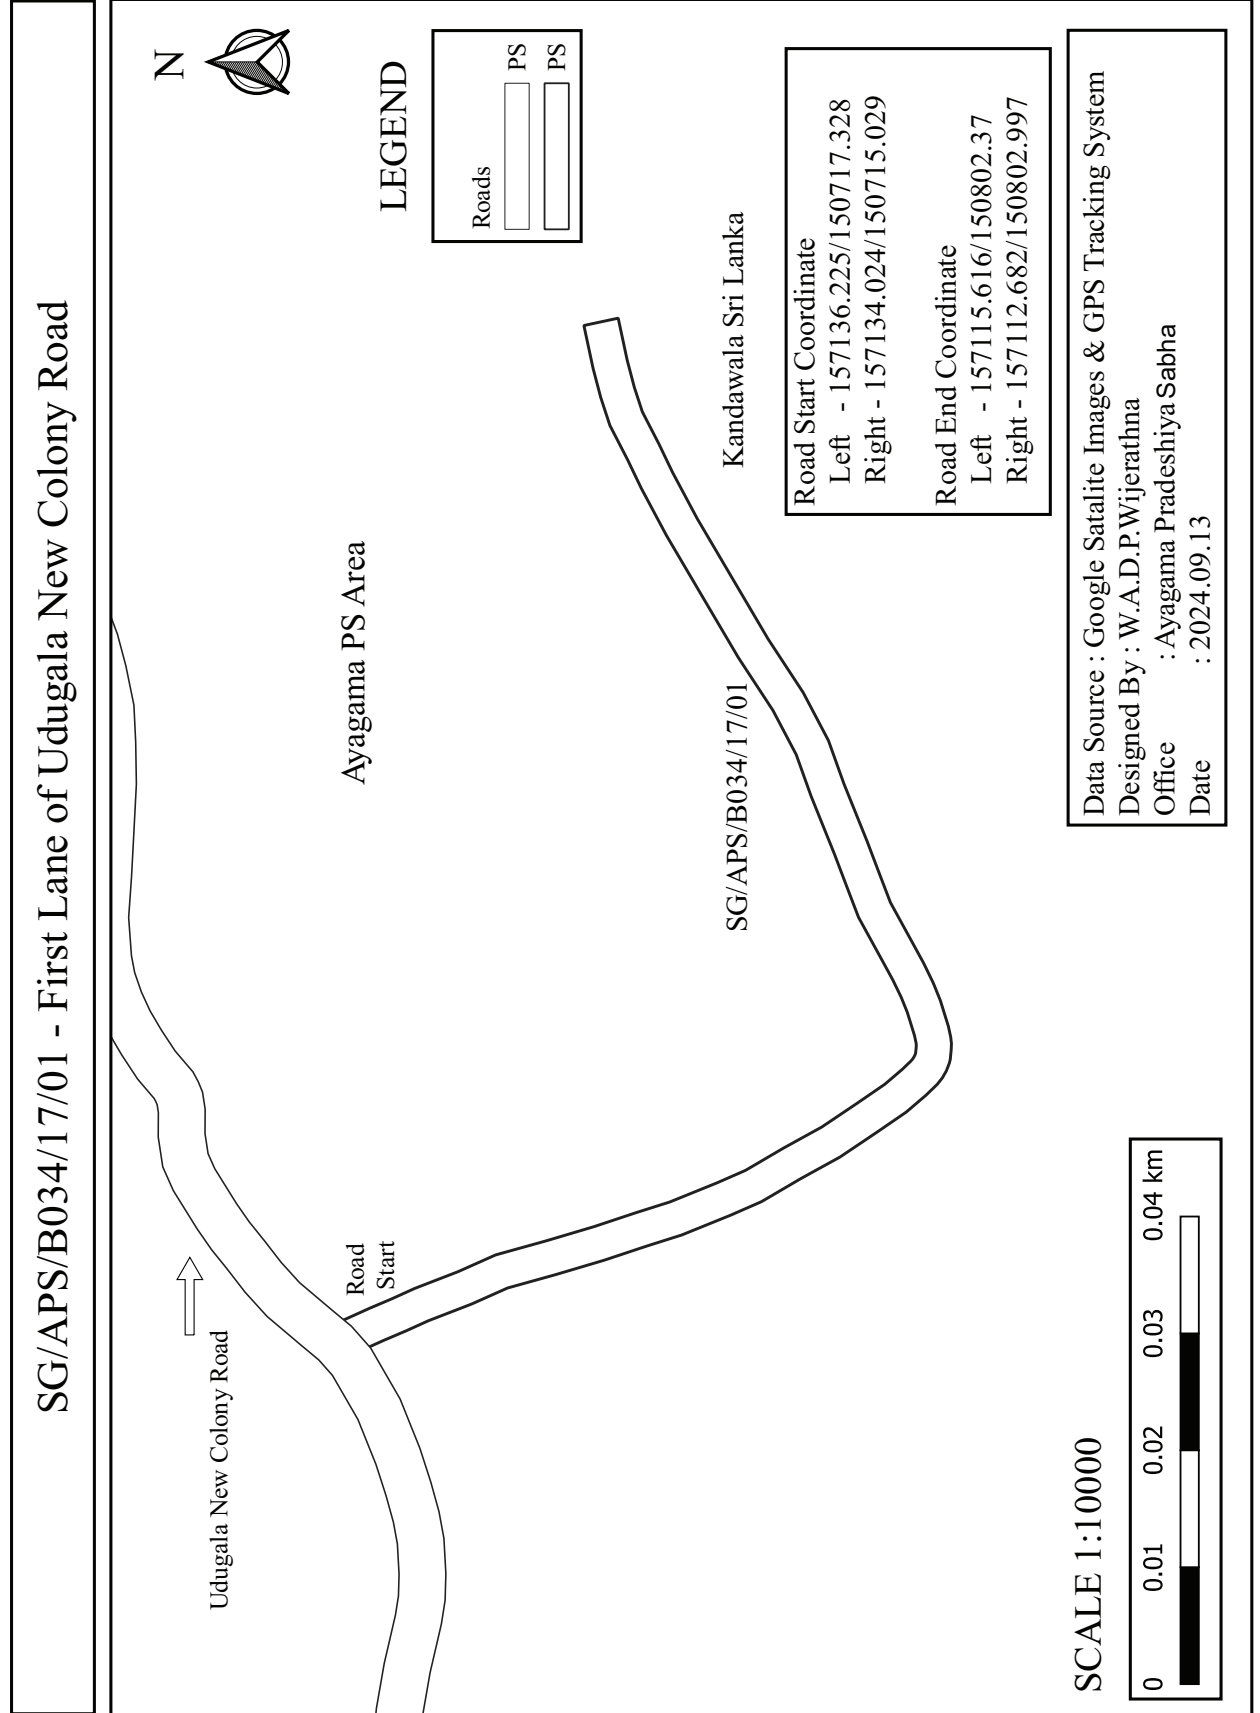


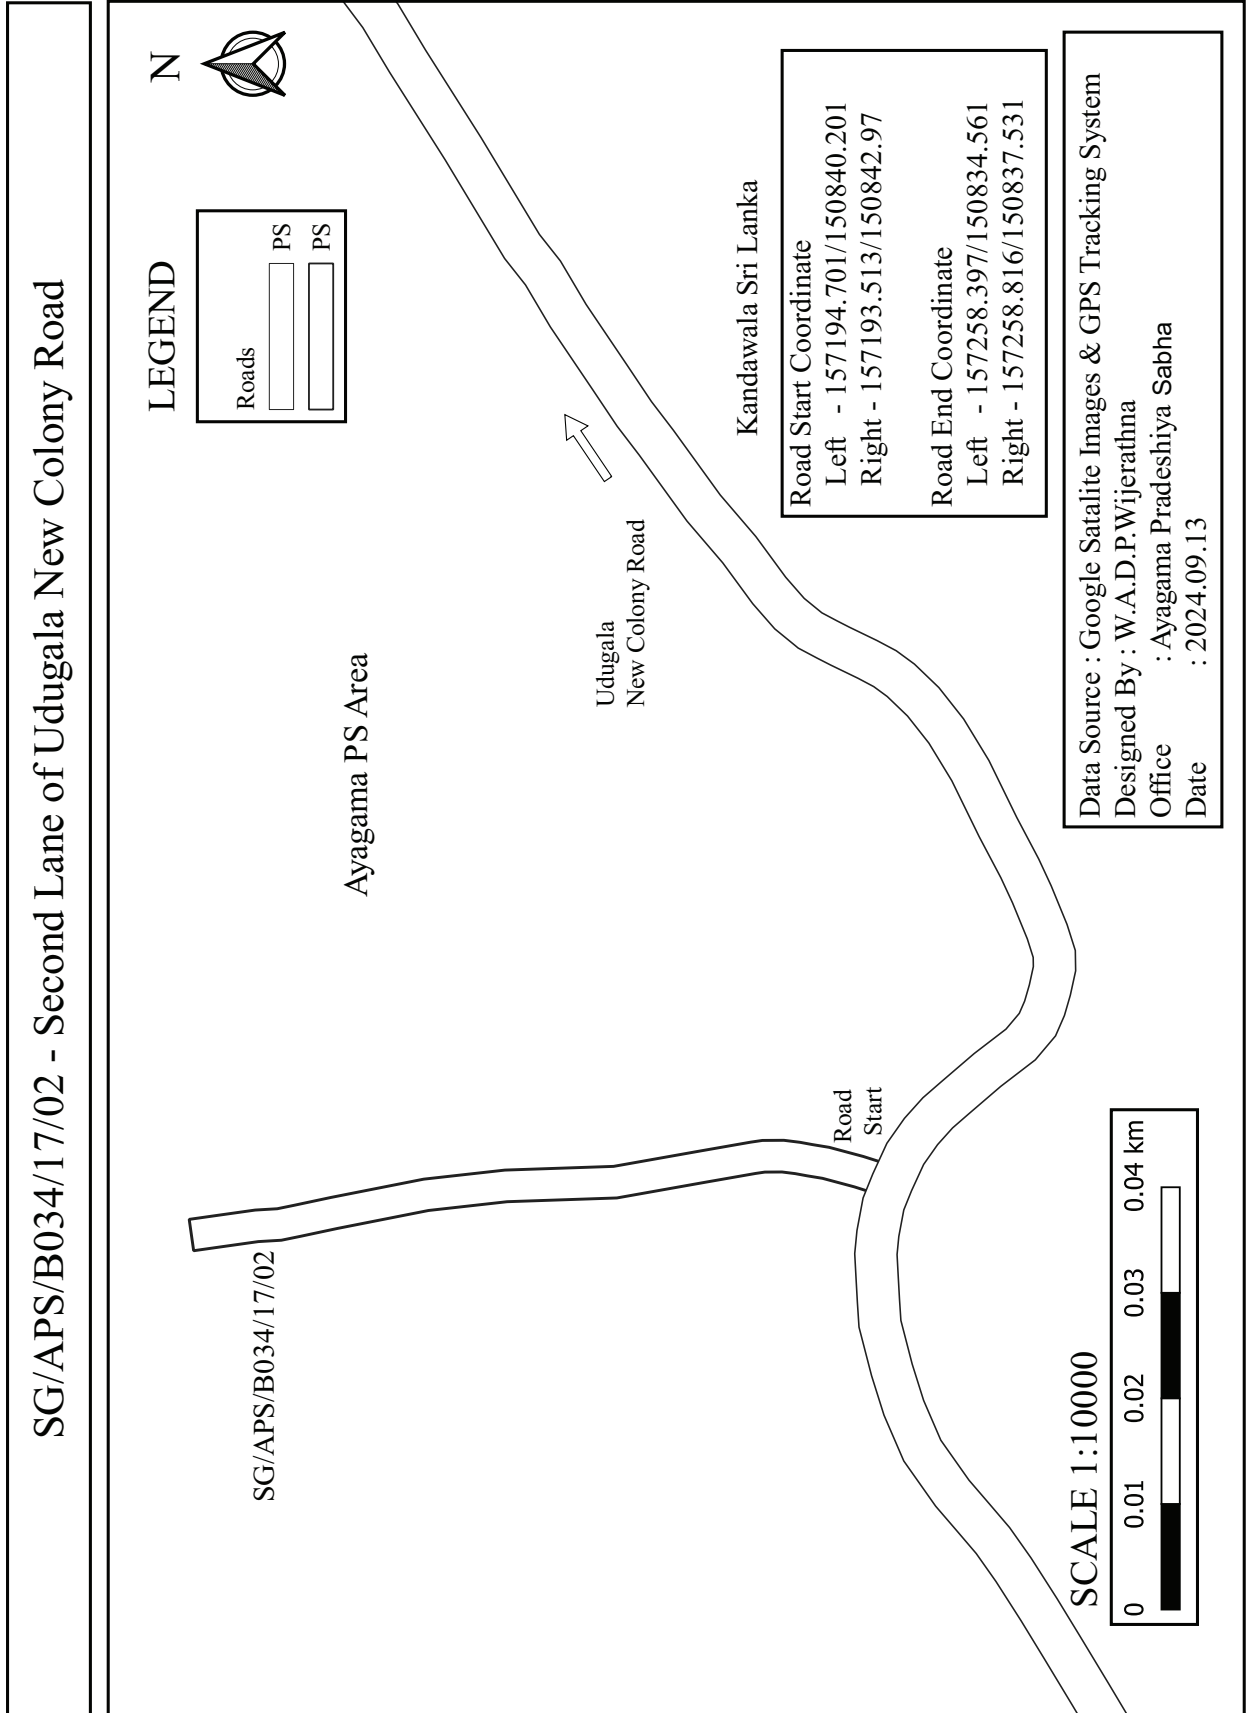


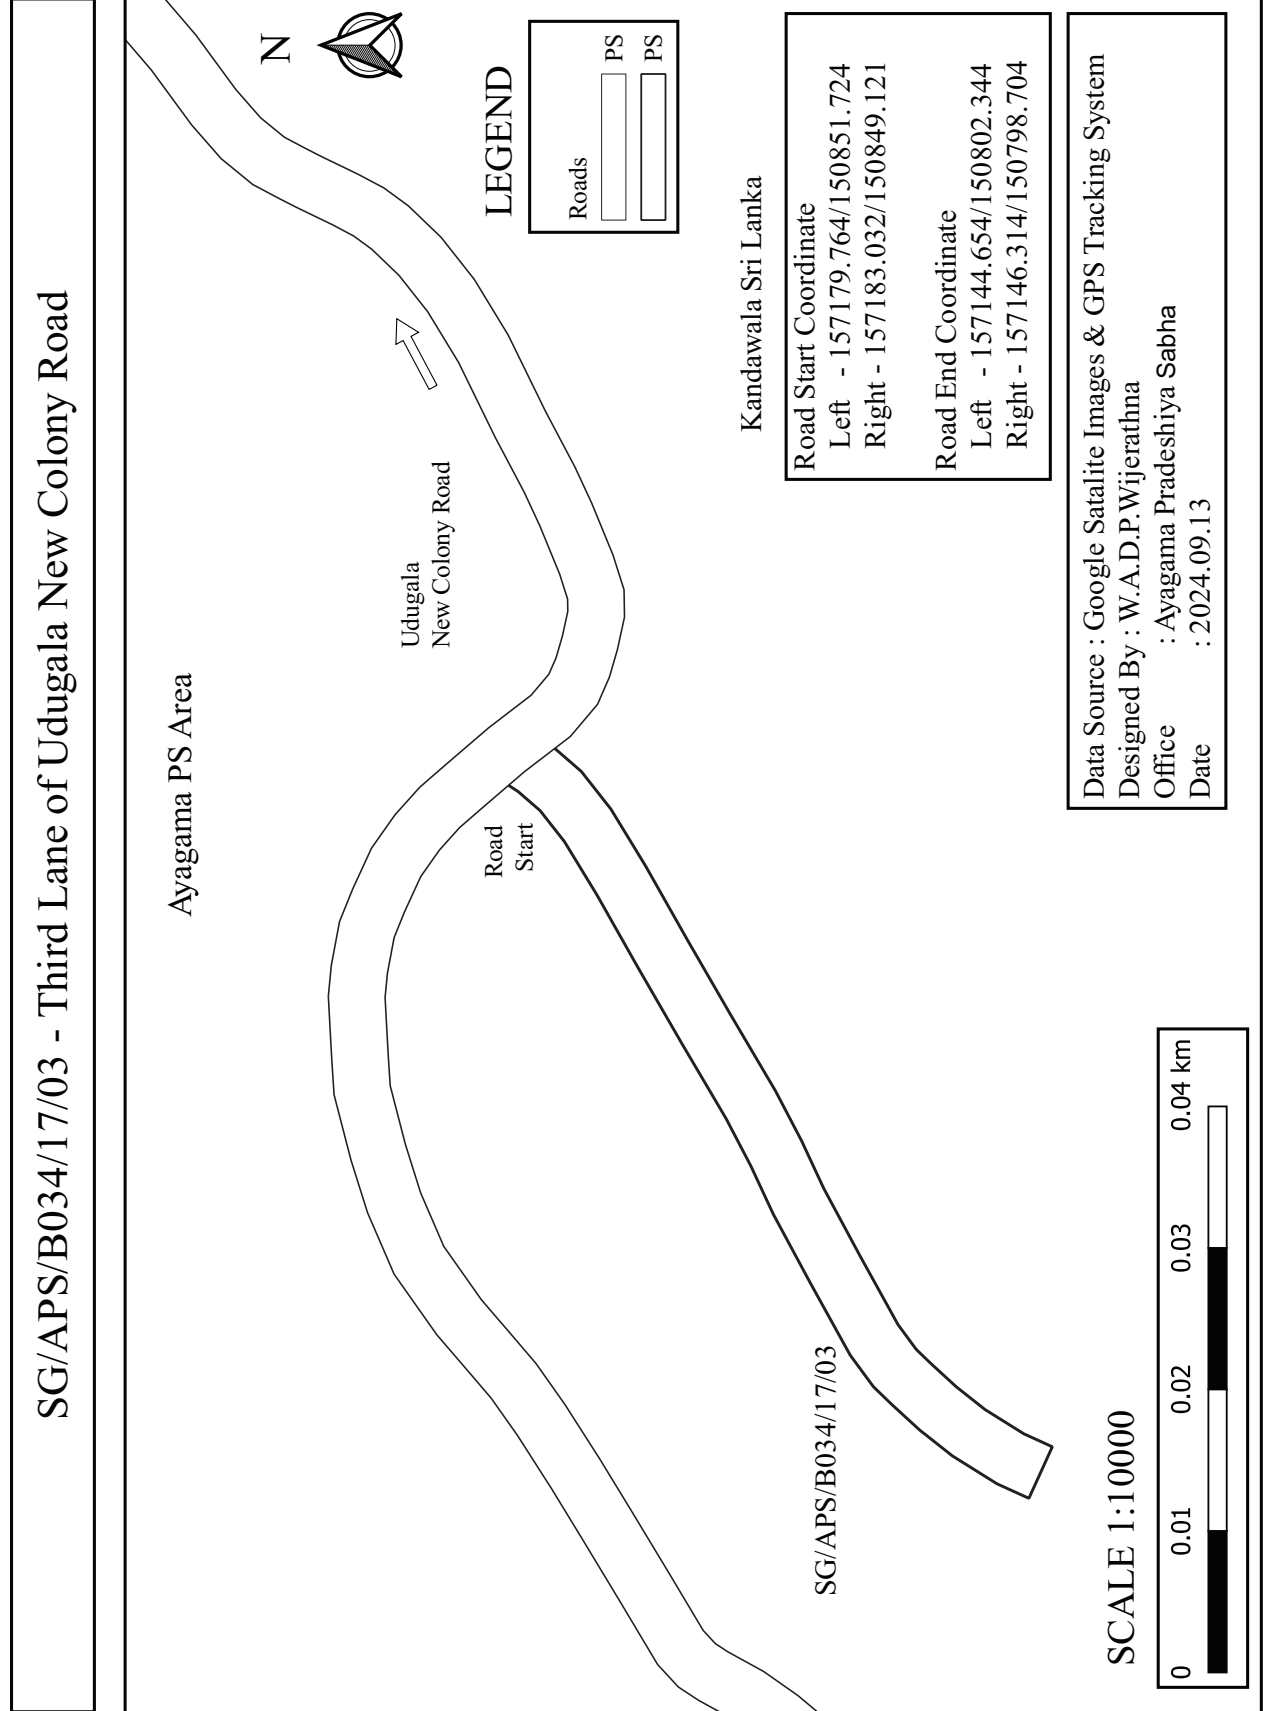


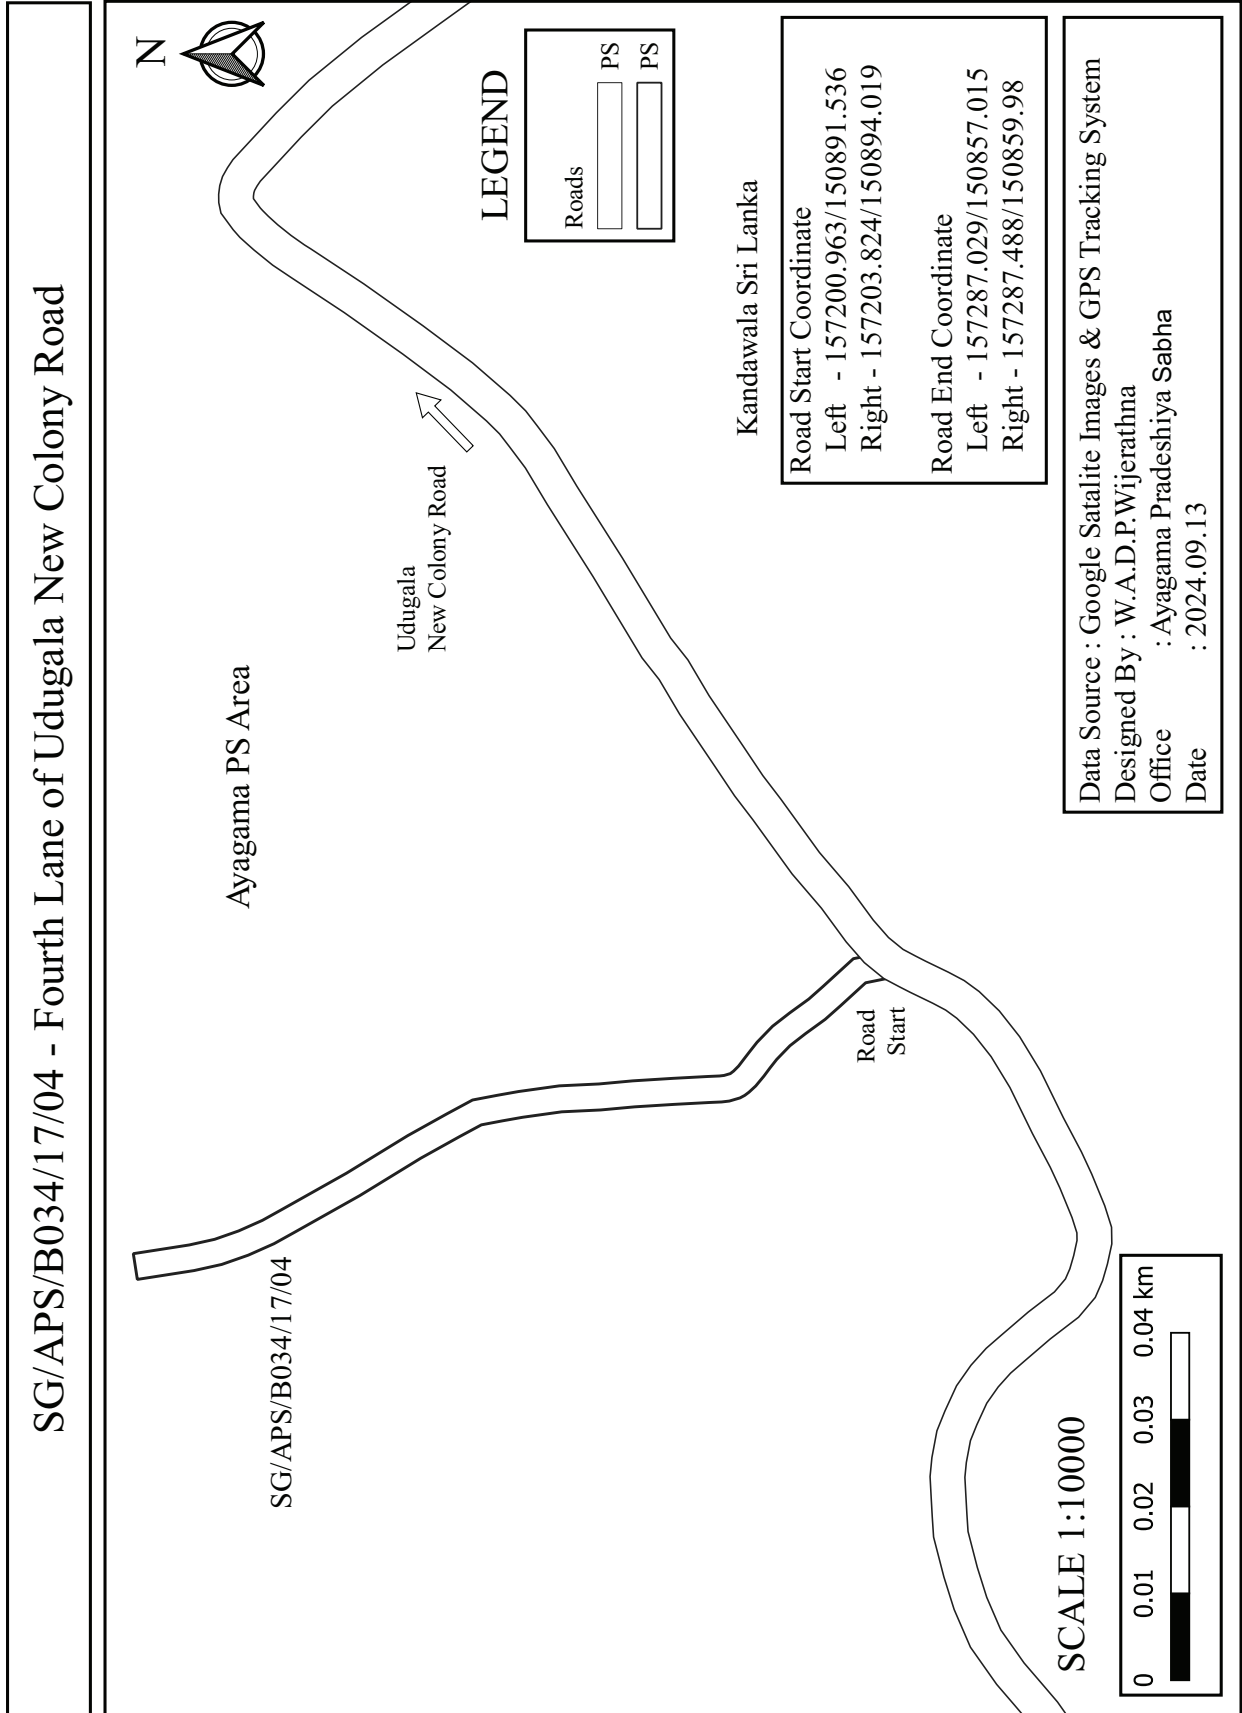


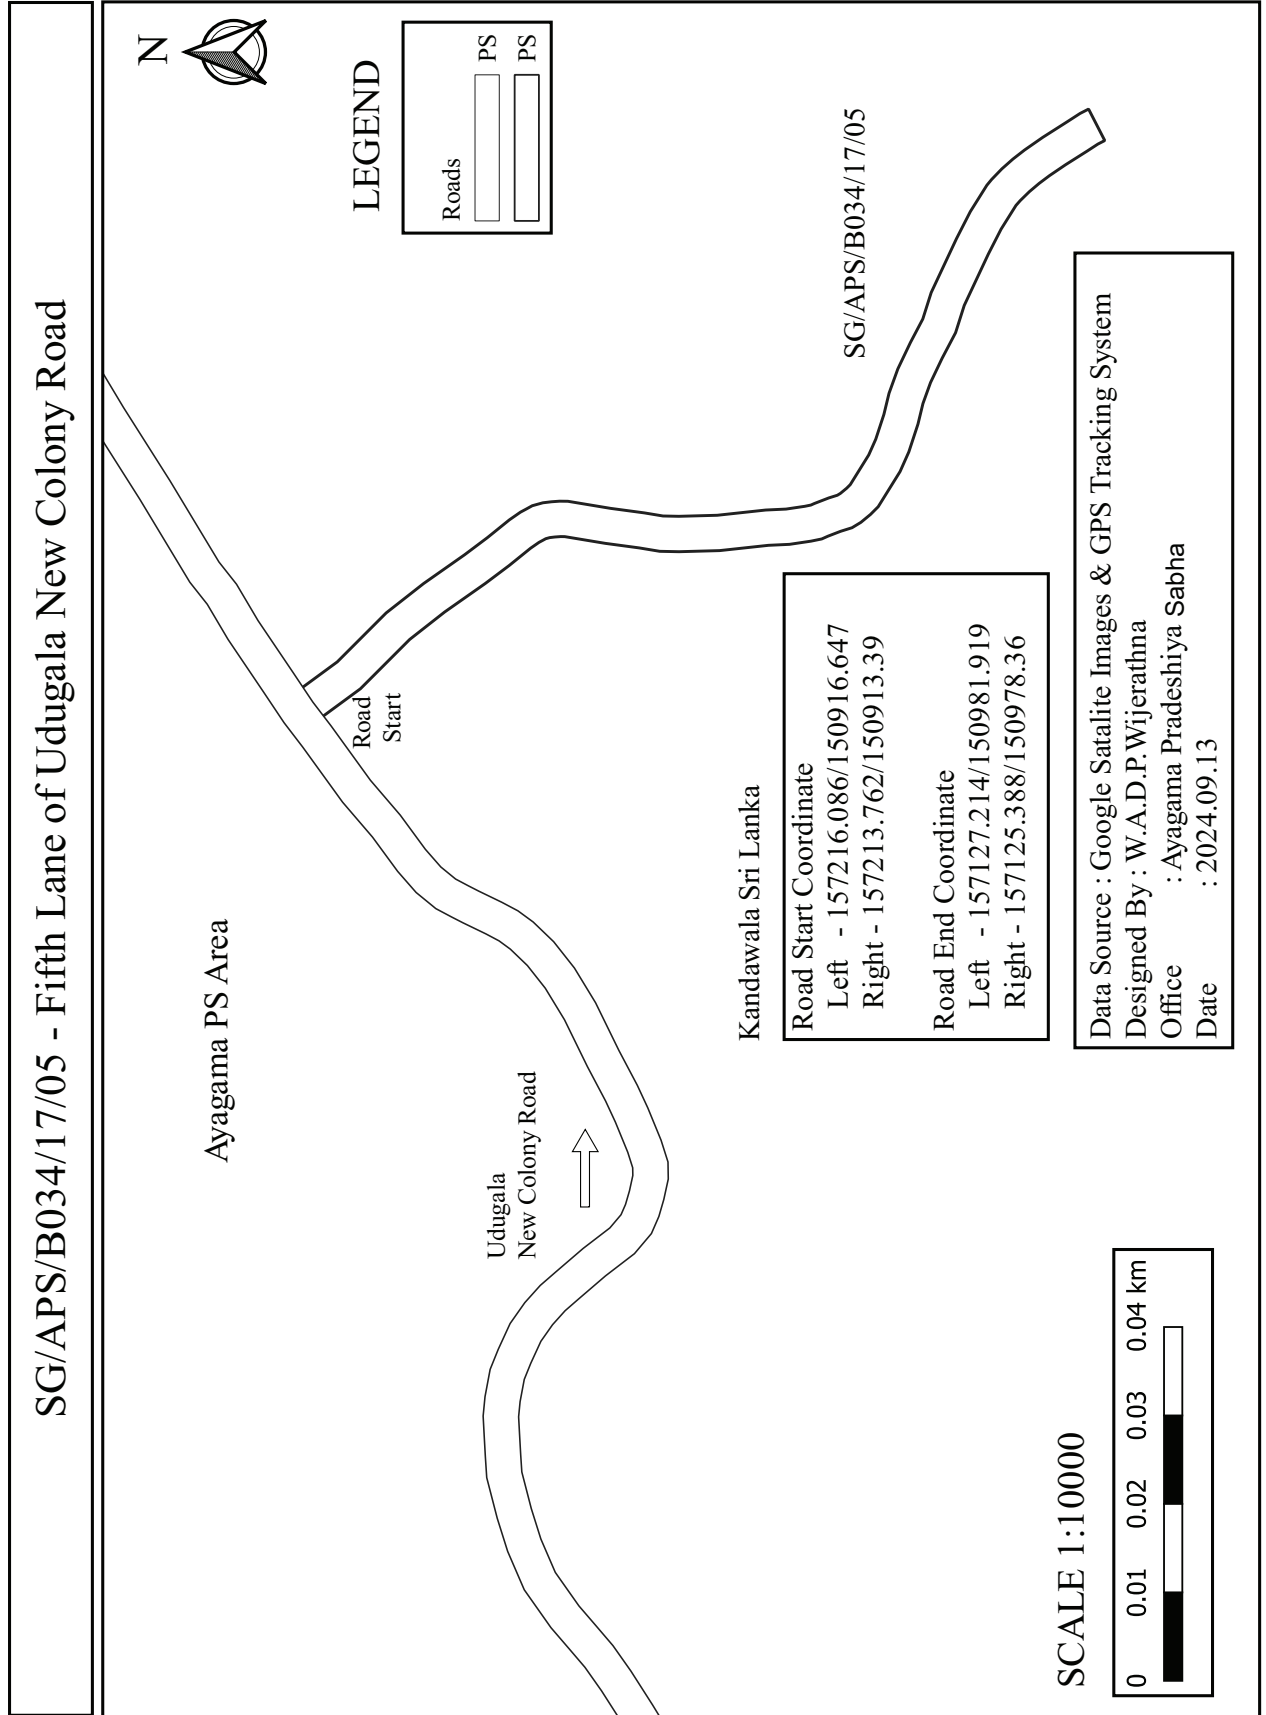

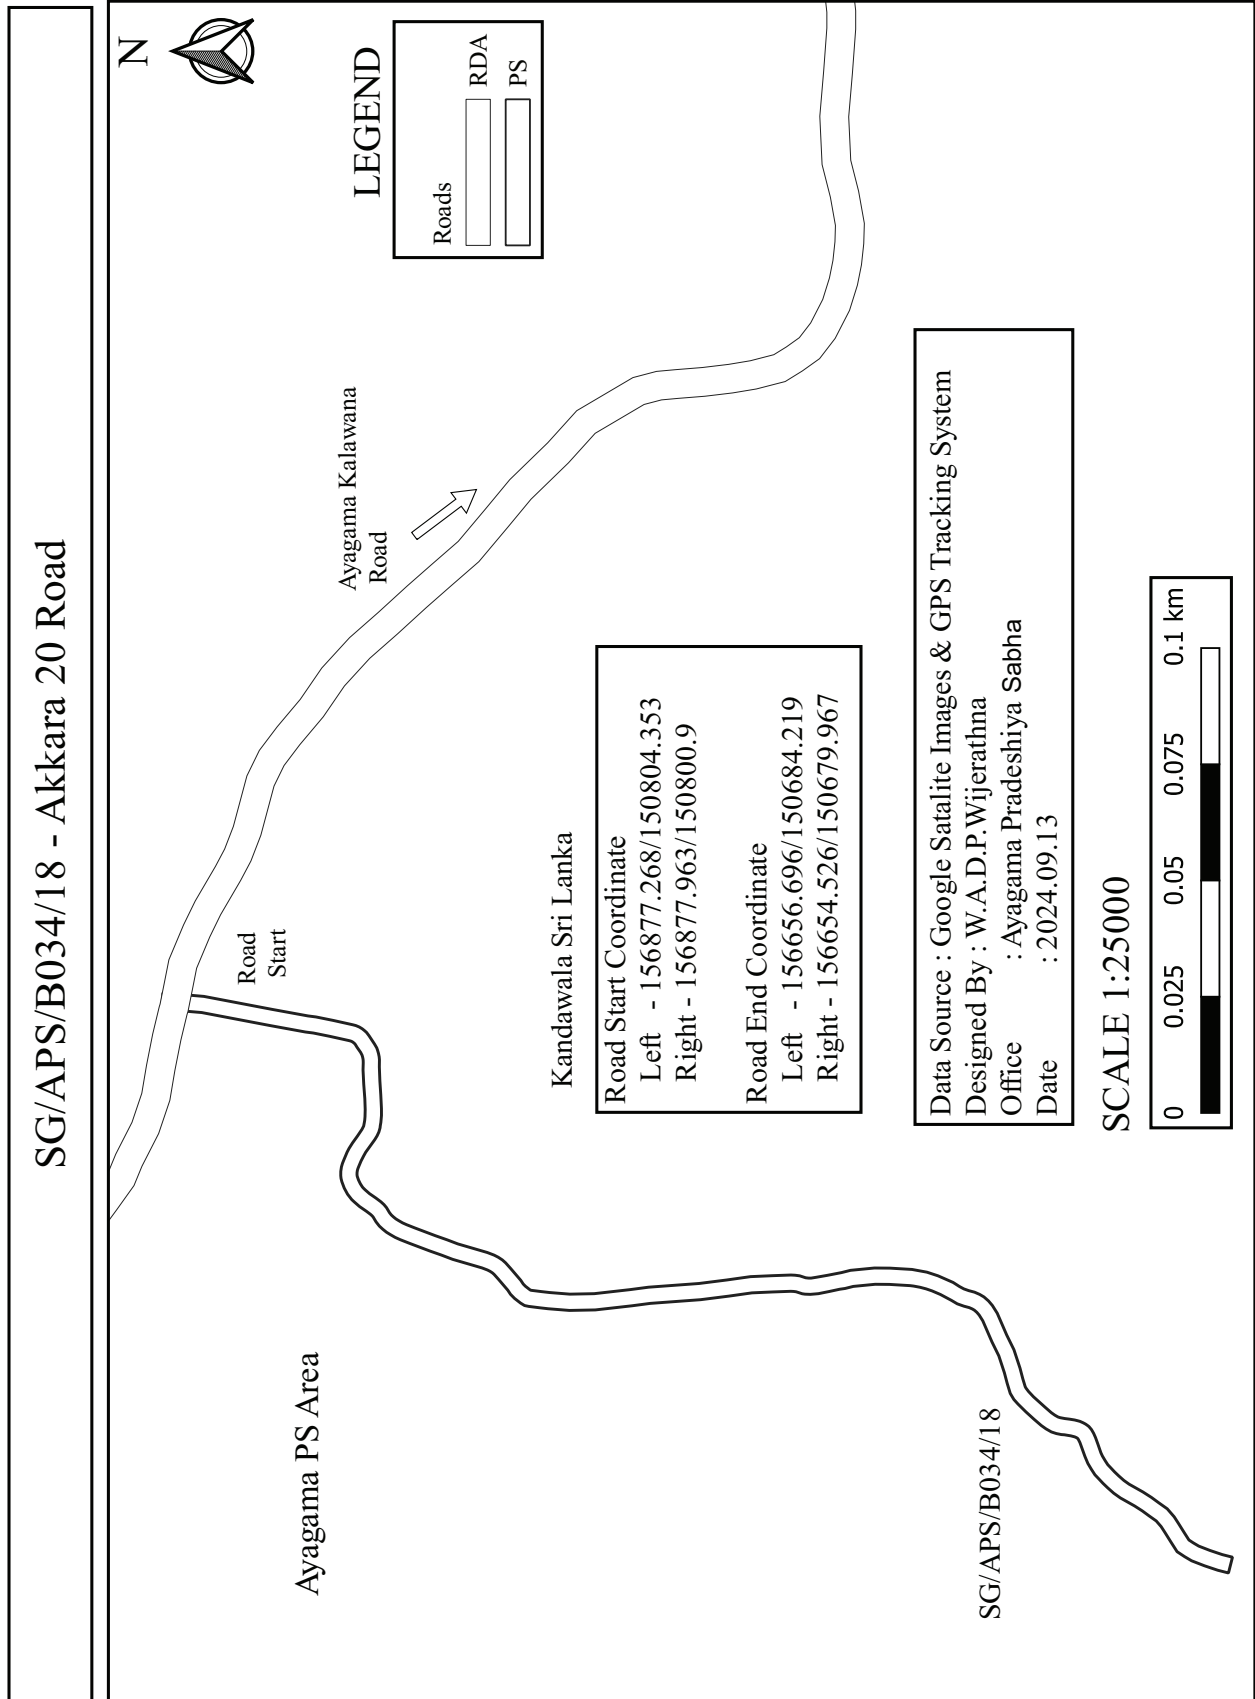

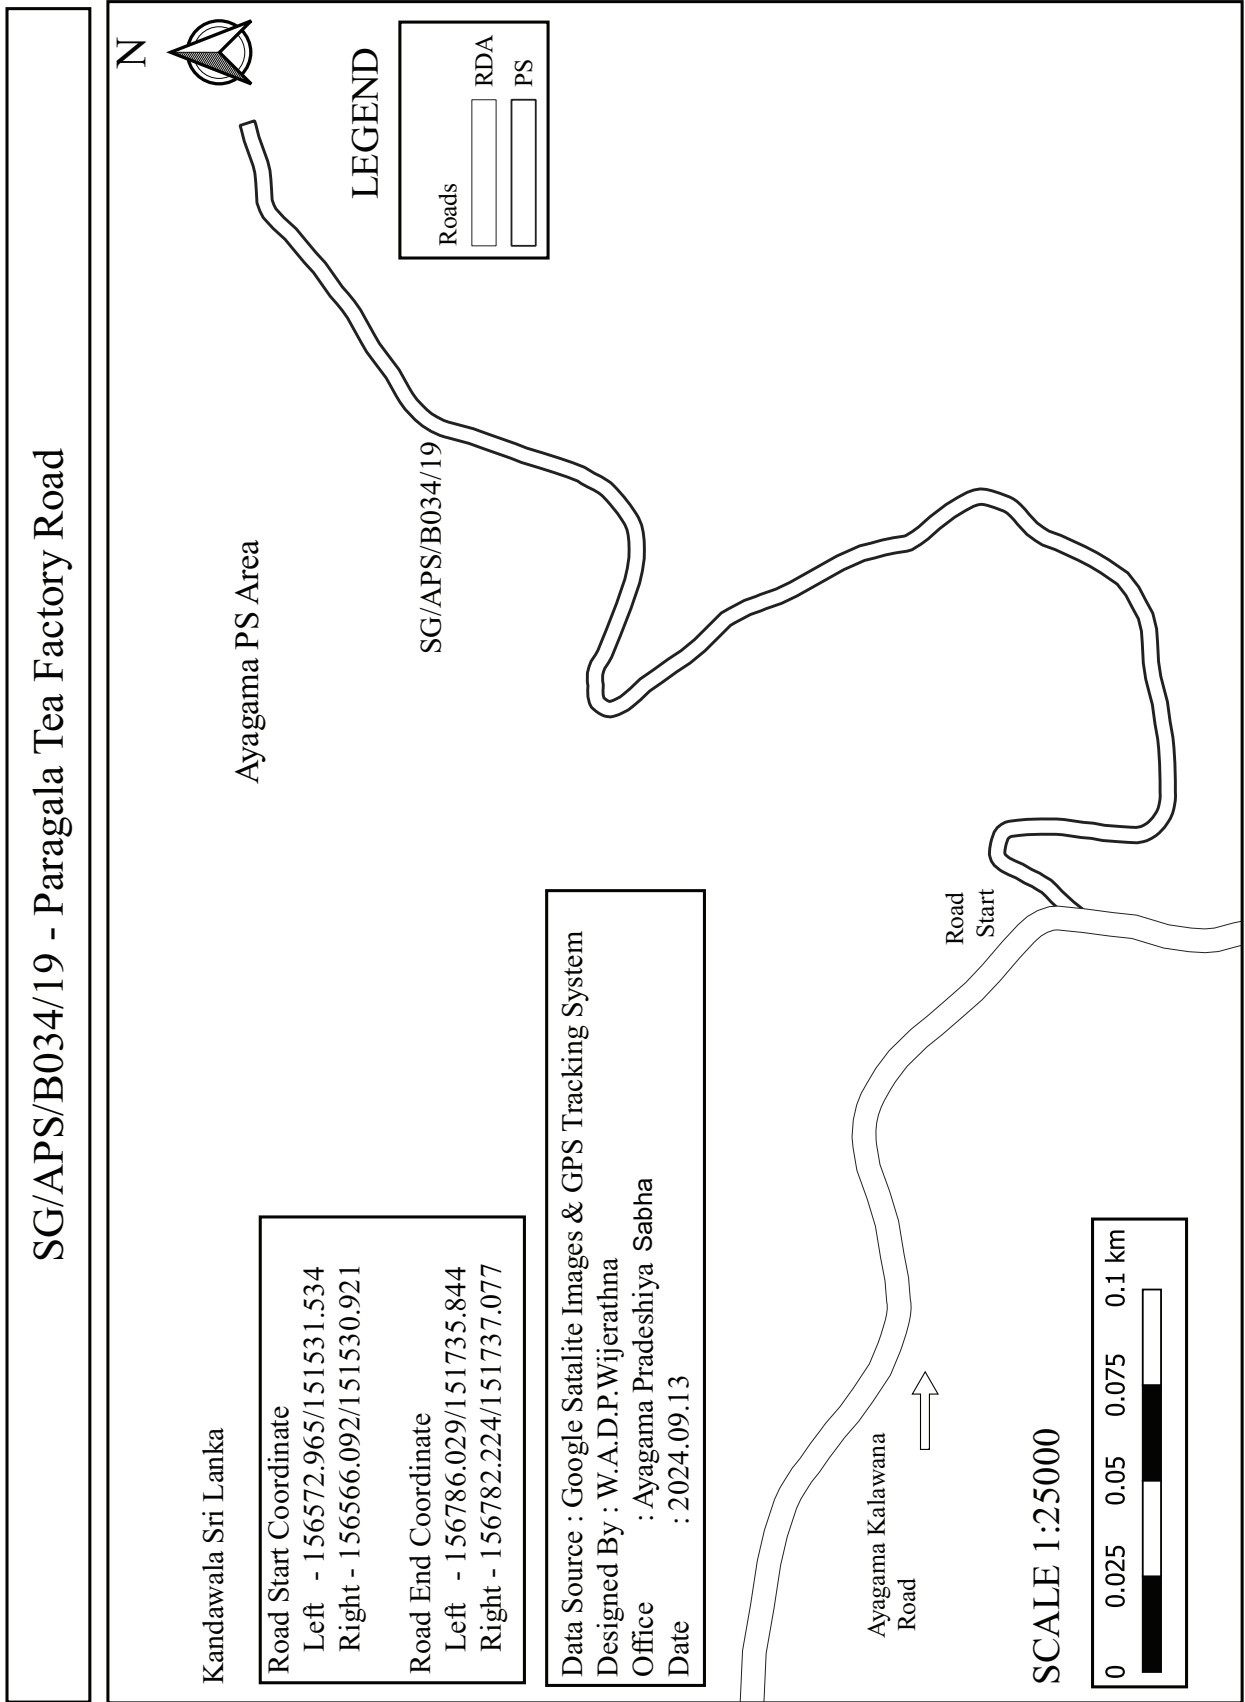

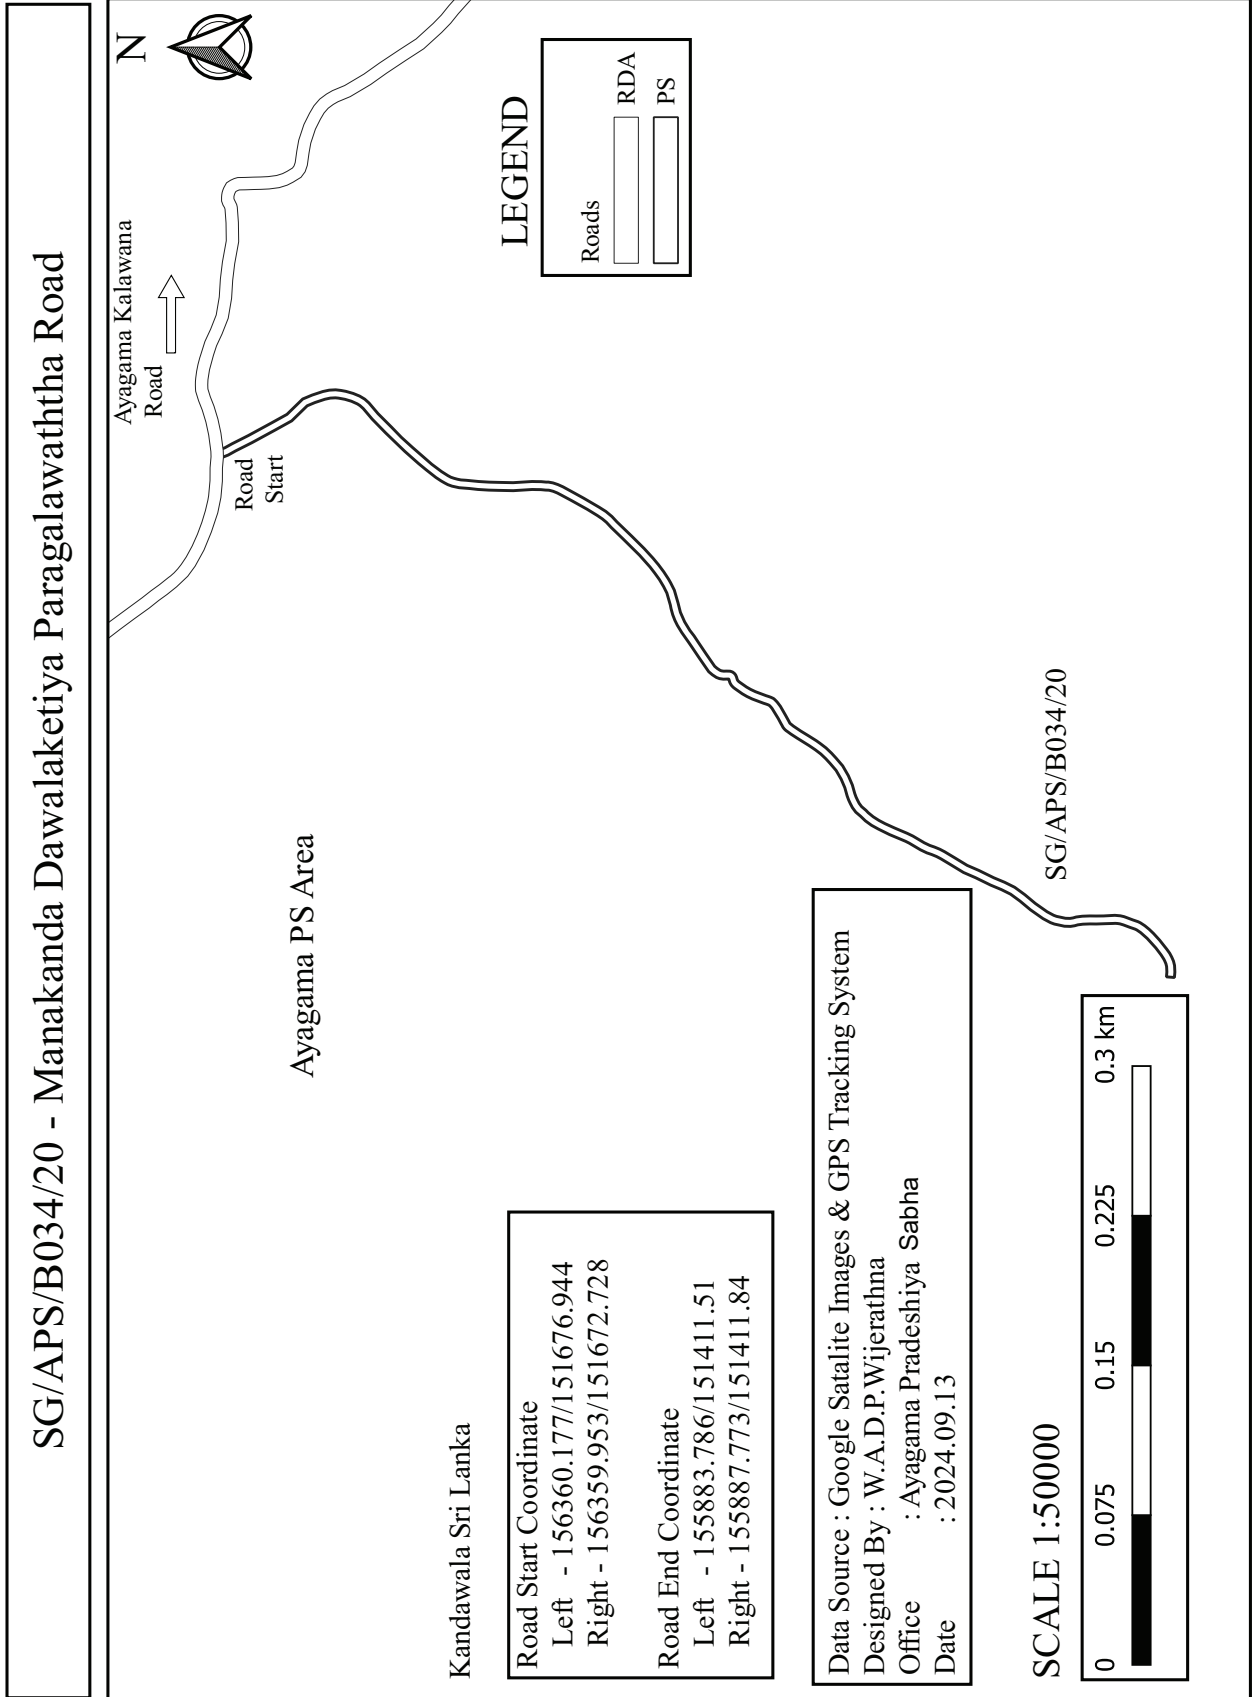

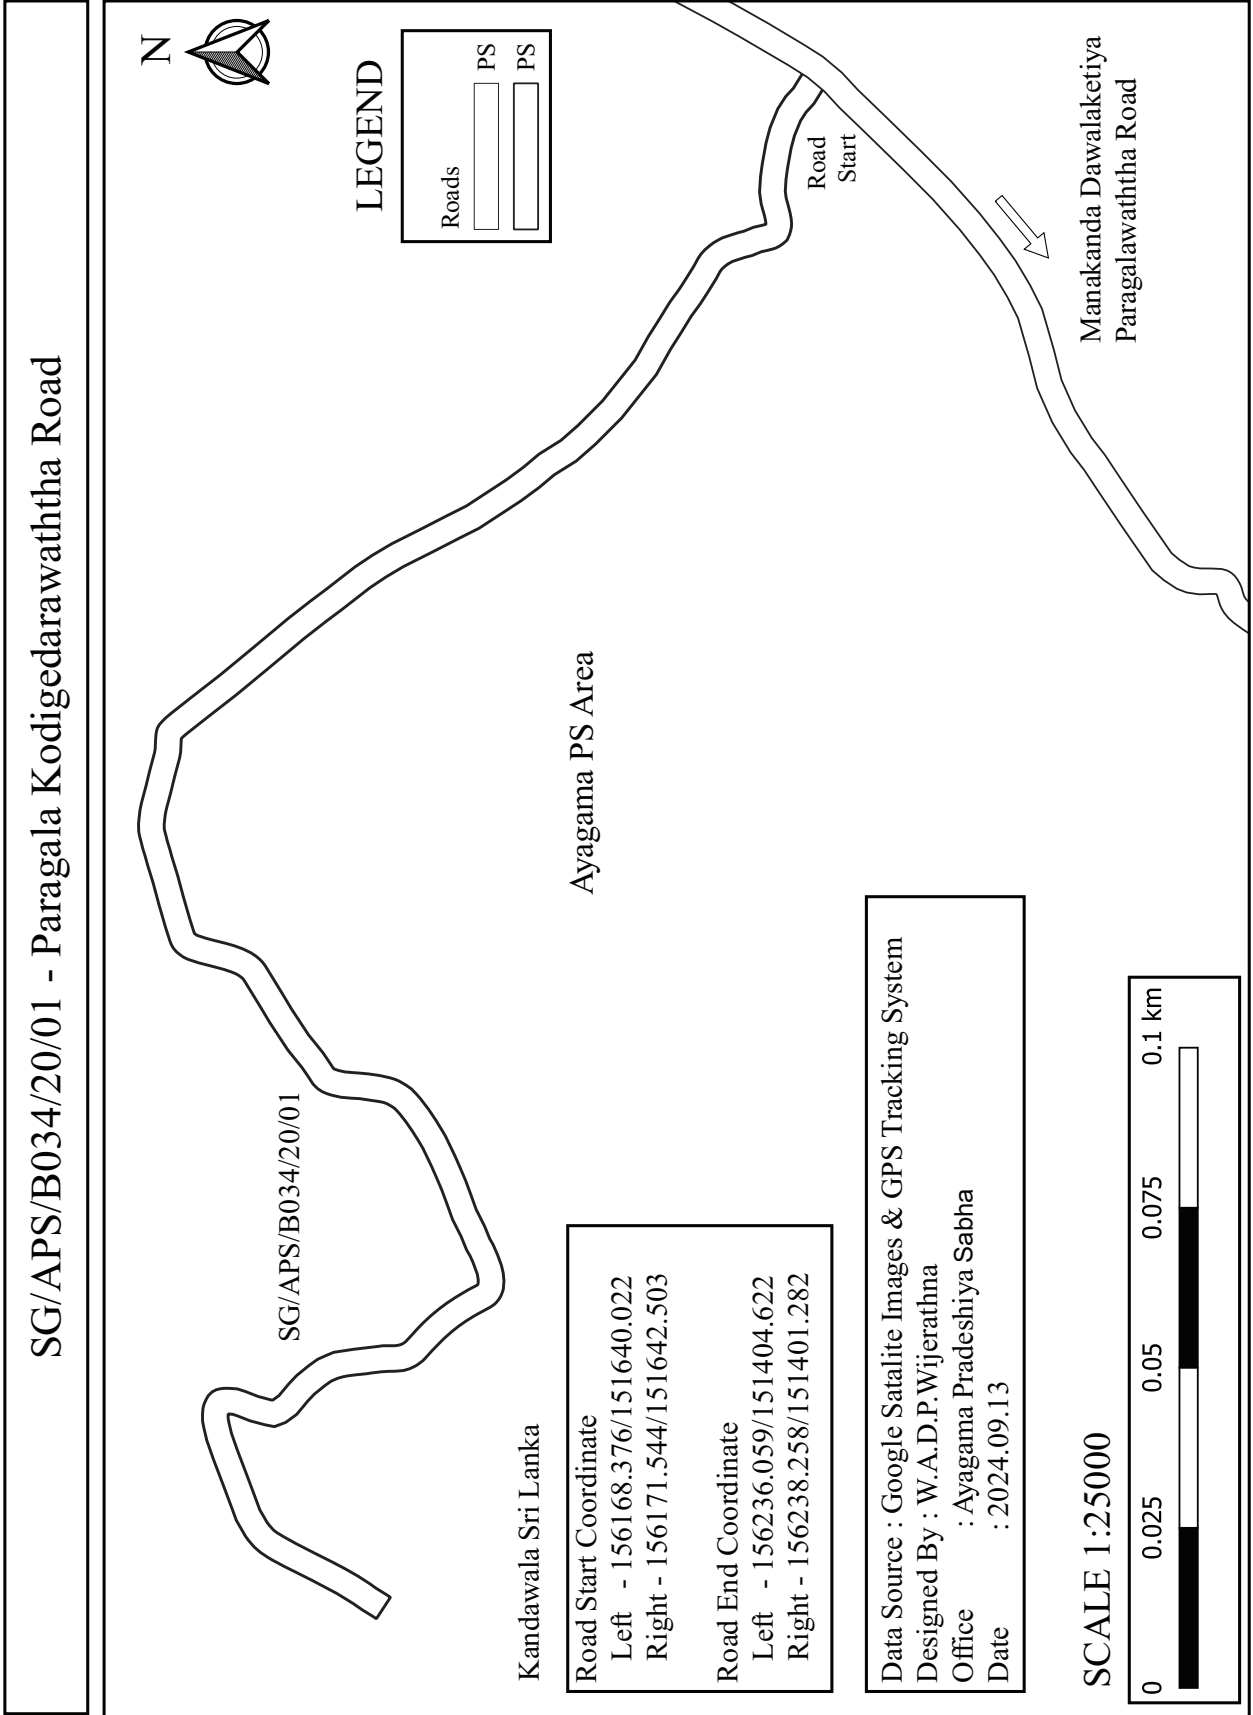

SG/APS/B034/20/02 - Paragala Manakanda Road

Data Source : Google Satalite Images & GPS Tracking System
 Designed By : W.A.D.P.Wijerathna
 Office : Ayagama Pradeshiya Sabha
 Date : 2024.09.13

Ayagama PS Area

LEGEND

Roads

PS

PS

Kandawala Sri Lanka

Road Start Coordinate

Left - 156169.797/151646.132

Right - 156166.453/151643.627

Road End Coordinate

Left - 155789.695/151426.375

Right - 155792.419/151429.304

SCALE 1:25000

0 0.025 0.05 0.075 0.1 km

Road
StartManakanda Dawalaketiya
Paragalawaththa Road

SG/APS/B034/20/02

SG/APS/B034/20/02/01 - Paragala Keselkotuwa Road

IV(අ) : කොටස - ශ්‍රී ලංකා ප්‍රජාතාන්ත්‍රික සමාජවාදී ජනරජයේ අති විශේෂ ගැසට් පත්‍රය - 2026.01.01
பகுதி IV(ஆ) - இலங்கைச் சனநாயக சோசலிசக் குடியரசு வர்த்தமானப் பத்திரிகை - அதி விசேஷமானது - 2026.01.01

127A



LEGEND

Roads		PS
		PS

Ayagama PS Area

Kandawala Sri Lanka

Road Start Coordinate
Left - 156157.289/151679.199
Right - 1156154.634/151682.46
Road End Coordinate
Left - 156034.065/151783.759
Right - 156034.102/151780.759

Data Source : Google Satalite Images & GPS Tracking System
Designed By : W.A.D.P.Wijerathna
Office : Ayagama Pradeshiya Sabha
Date : 2024.09.13

Road
Start

Paragala
Manakanda Road




SG/APS/B034/20/02/01

SCALE 1:10000

0 0.01 0.02 0.03 0.04 km



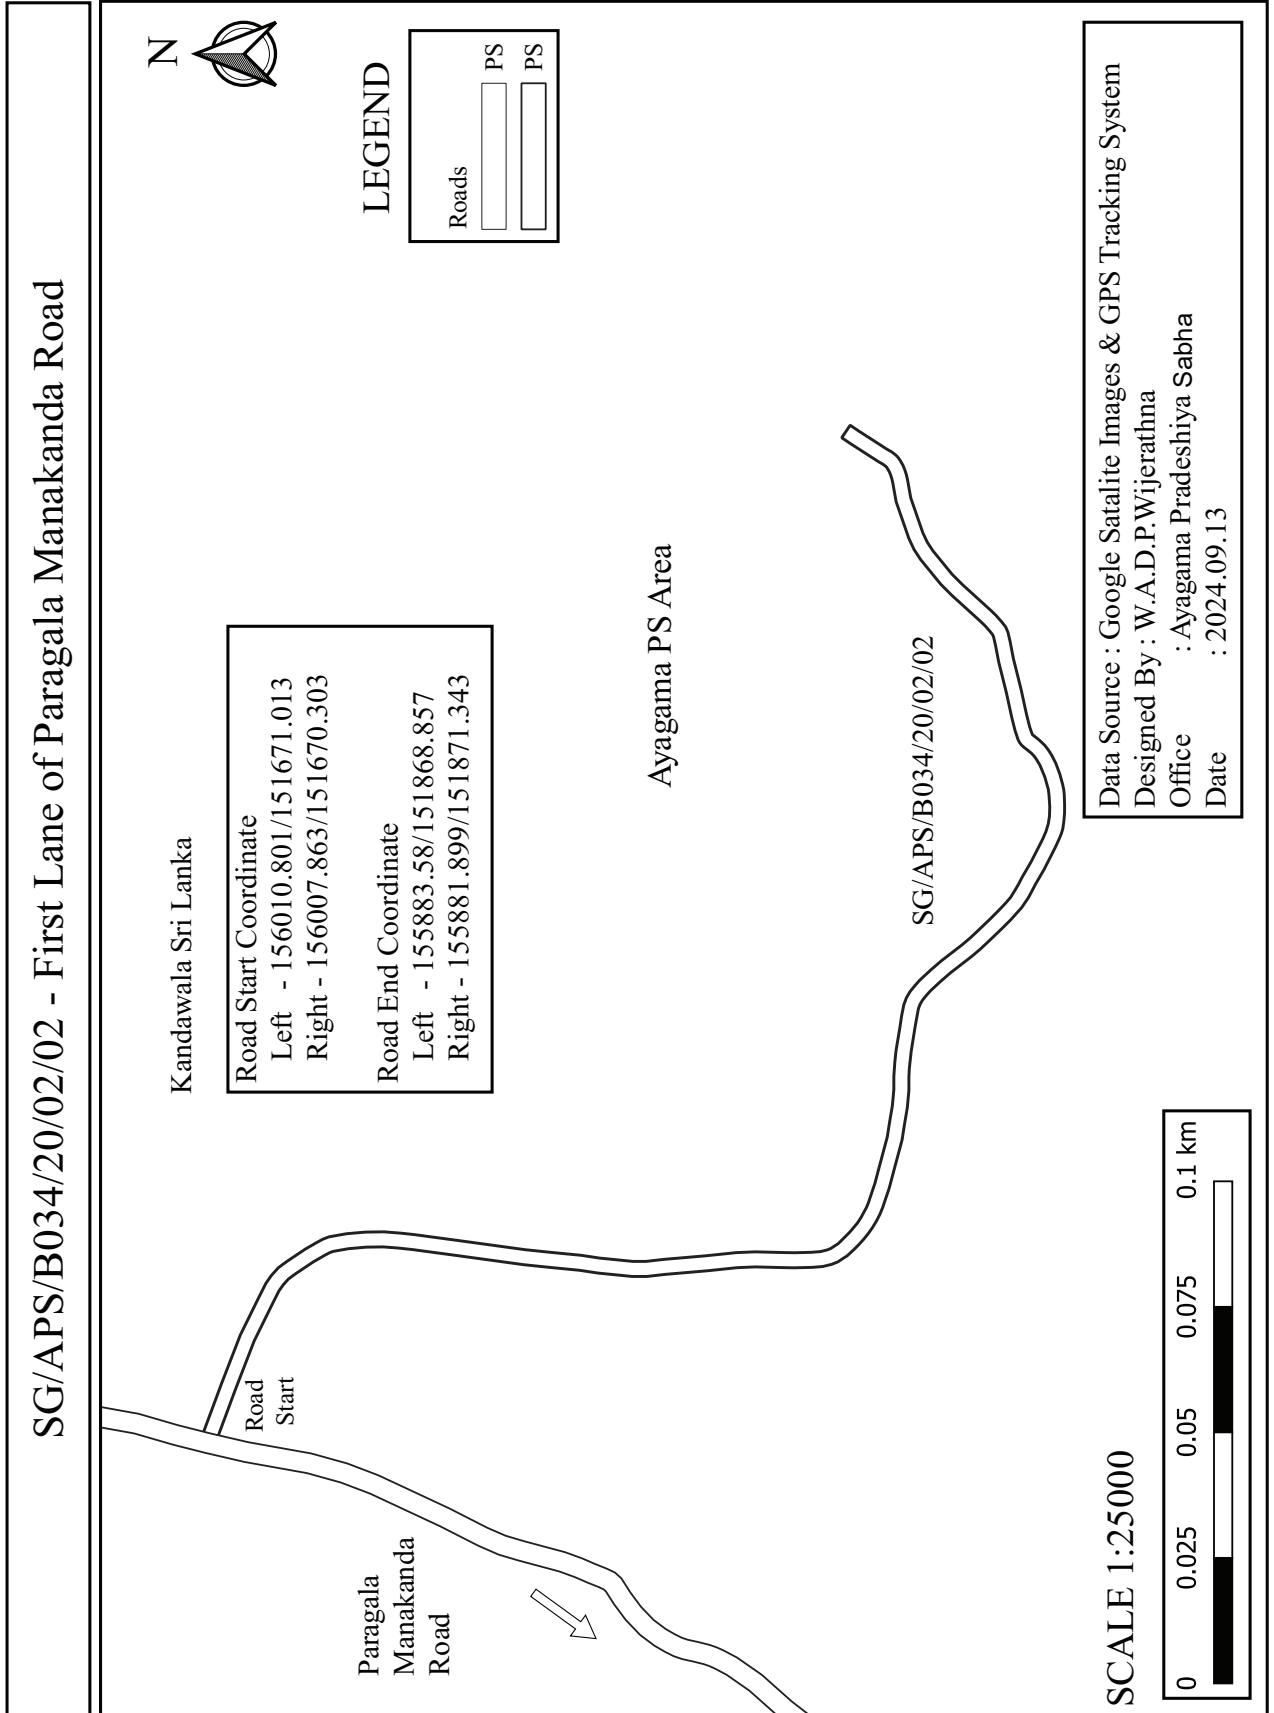

LEGEND

Roads

PS

PS

SG/APS/B034/20/02/03 - Paragalakanda Road

Paragala
Manakanda
Road

Road Start

Ayagama PS Area

SG/APS/B034/20/02/03

Kandawala Sri Lanka

Road Start Coordinate

Left - 155843.954/151581.64

Right - 155840.732/151579.269

Road End Coordinate

Left - 155314.994/151842.066

Right - 155311.916/151839.512

Data Source : Google Satalite Images & GPS Tracking System

Designed By : W.A.D.P.Wijerathna

Office : Ayagama Pradeshiya Sabha


Date : 2024.09.13


SCALE 1:50000


0	0.075	0.15	0.225	0.3 km
---	-------	------	-------	--------

0.3 km

0.3 km

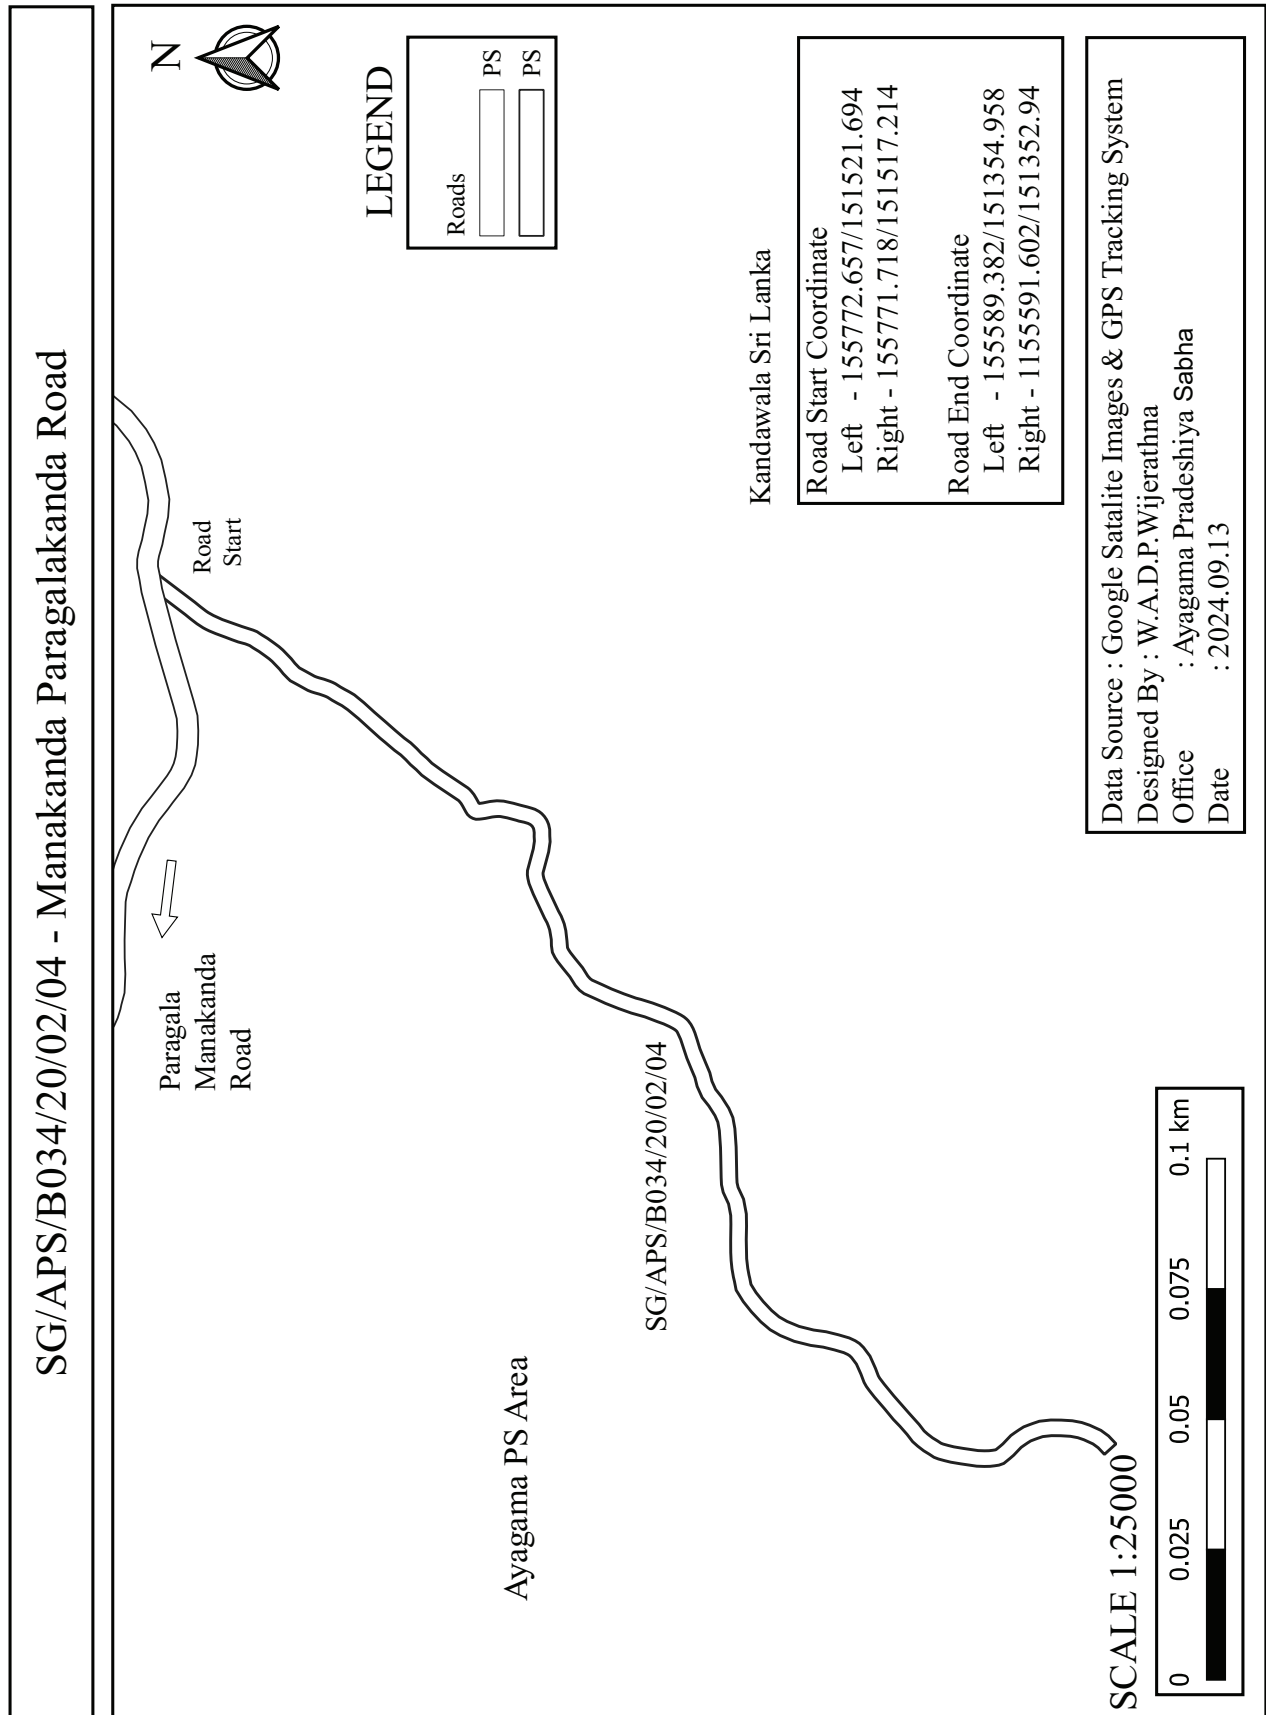

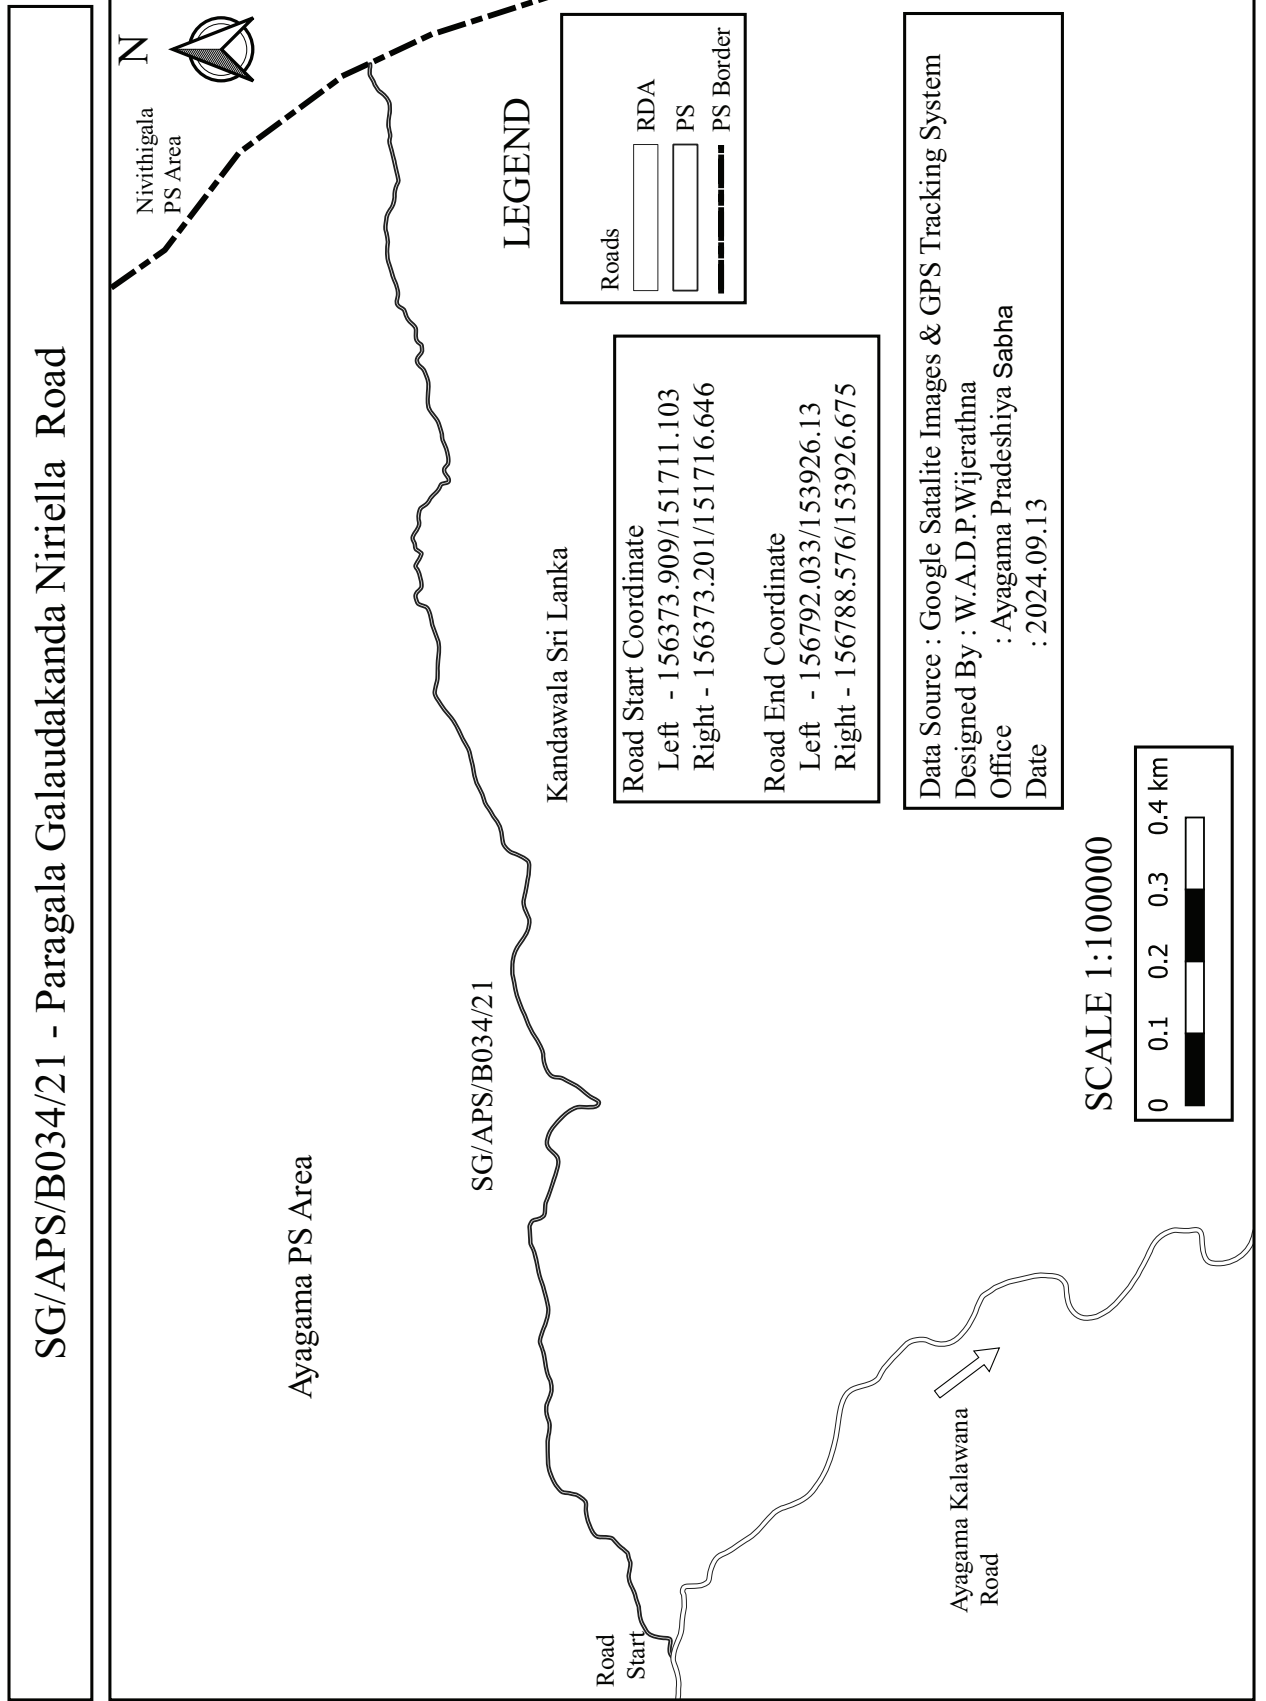

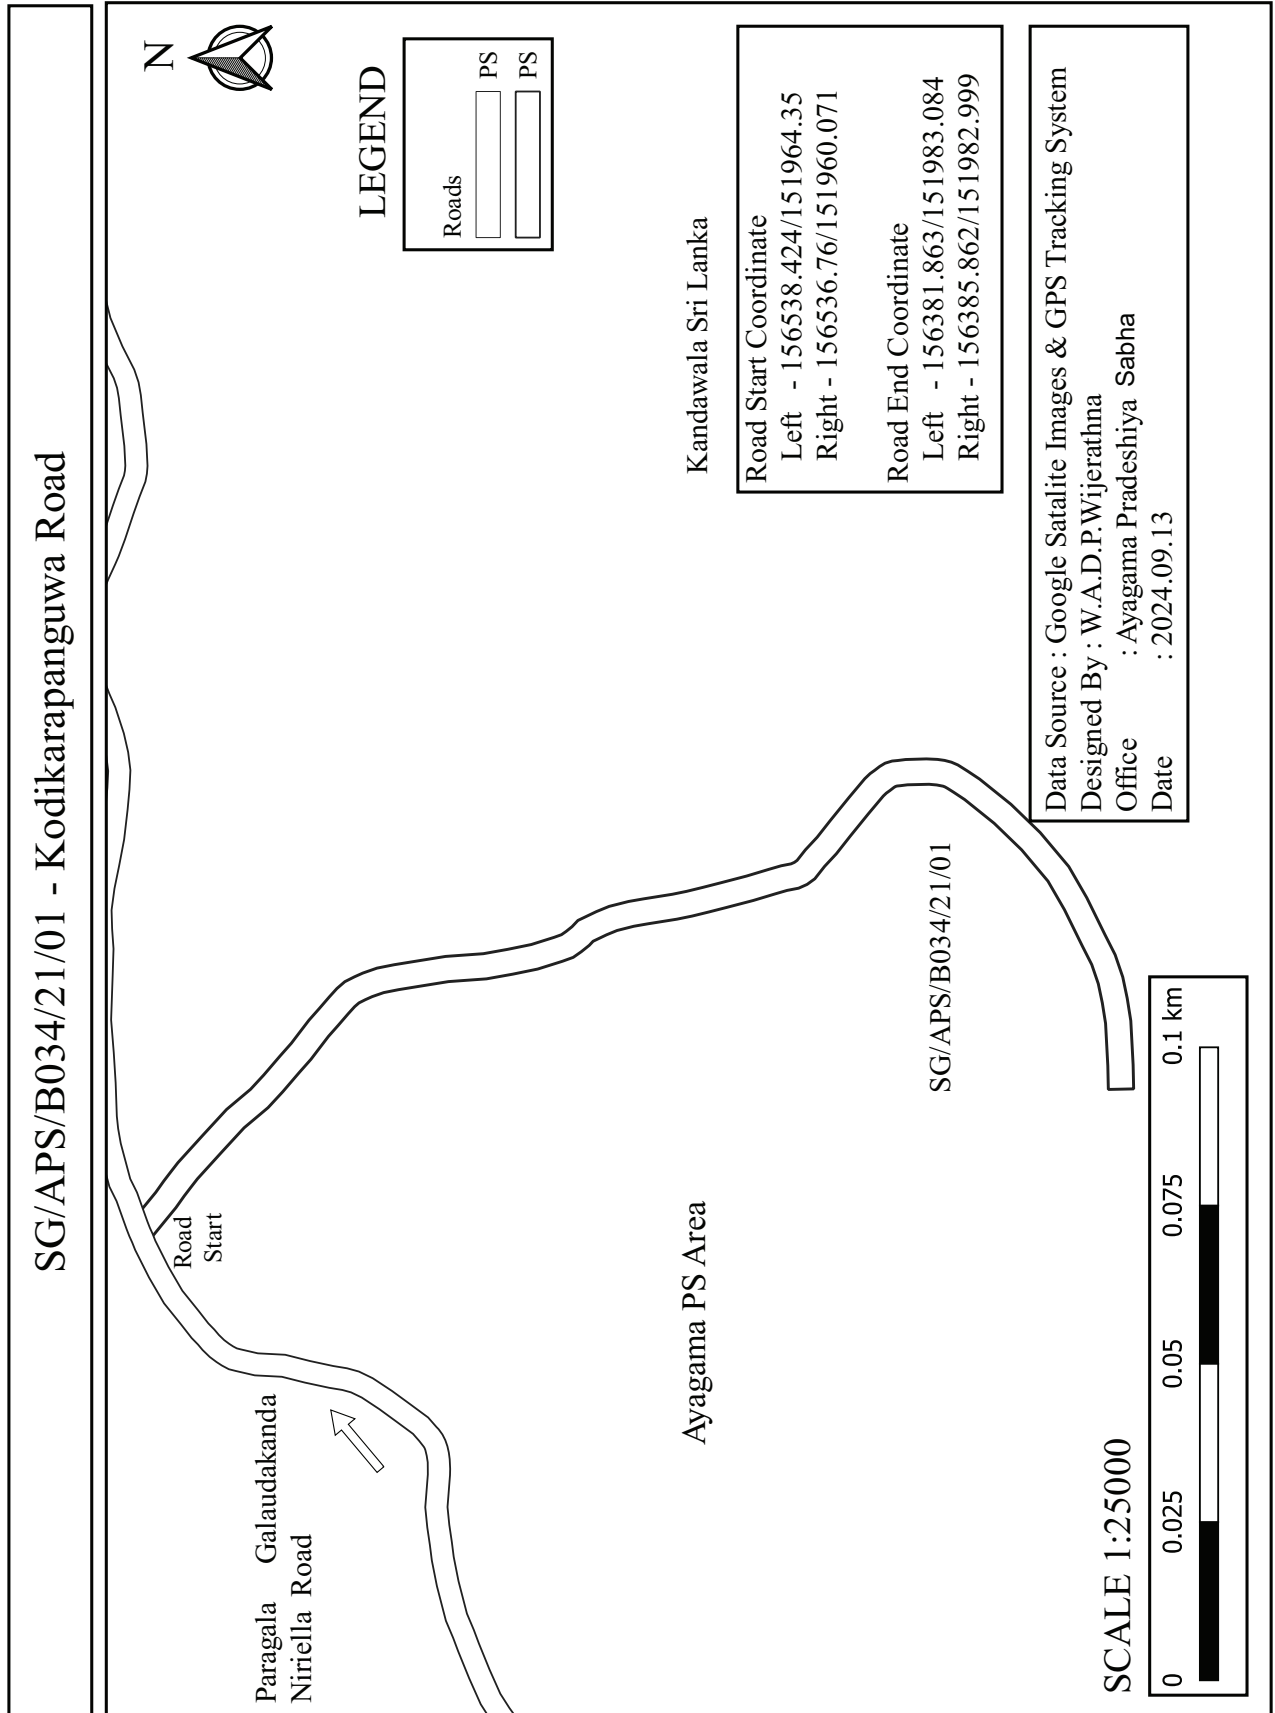

LEGEND

Roads

ps

PS

SG/APS/B034/21/02 - Kiwulahena Kodikarapanguwa Road

SG/APS/B034/21/02

Ayagama PS Area

Kandawala Sri Lanka

Road Start Coordinate

Left - 156546.391/152043.263

Right - 156548.149/152048.114

Road End Coordinate

Left - 156787.385/151893.95

Right - 156791.09/151895.46

Data Source : Google Satalite Images & GPS Tracking System

Designed By : W.A.D.P.Wijerathna


Office : Ayagama Pradeshiya Sabha


Date : 2024.09.13


SCALE 1:25000


0 0.025 0.05 0.075 0.1 km


Paragala Galaudakanda
Niriella Road

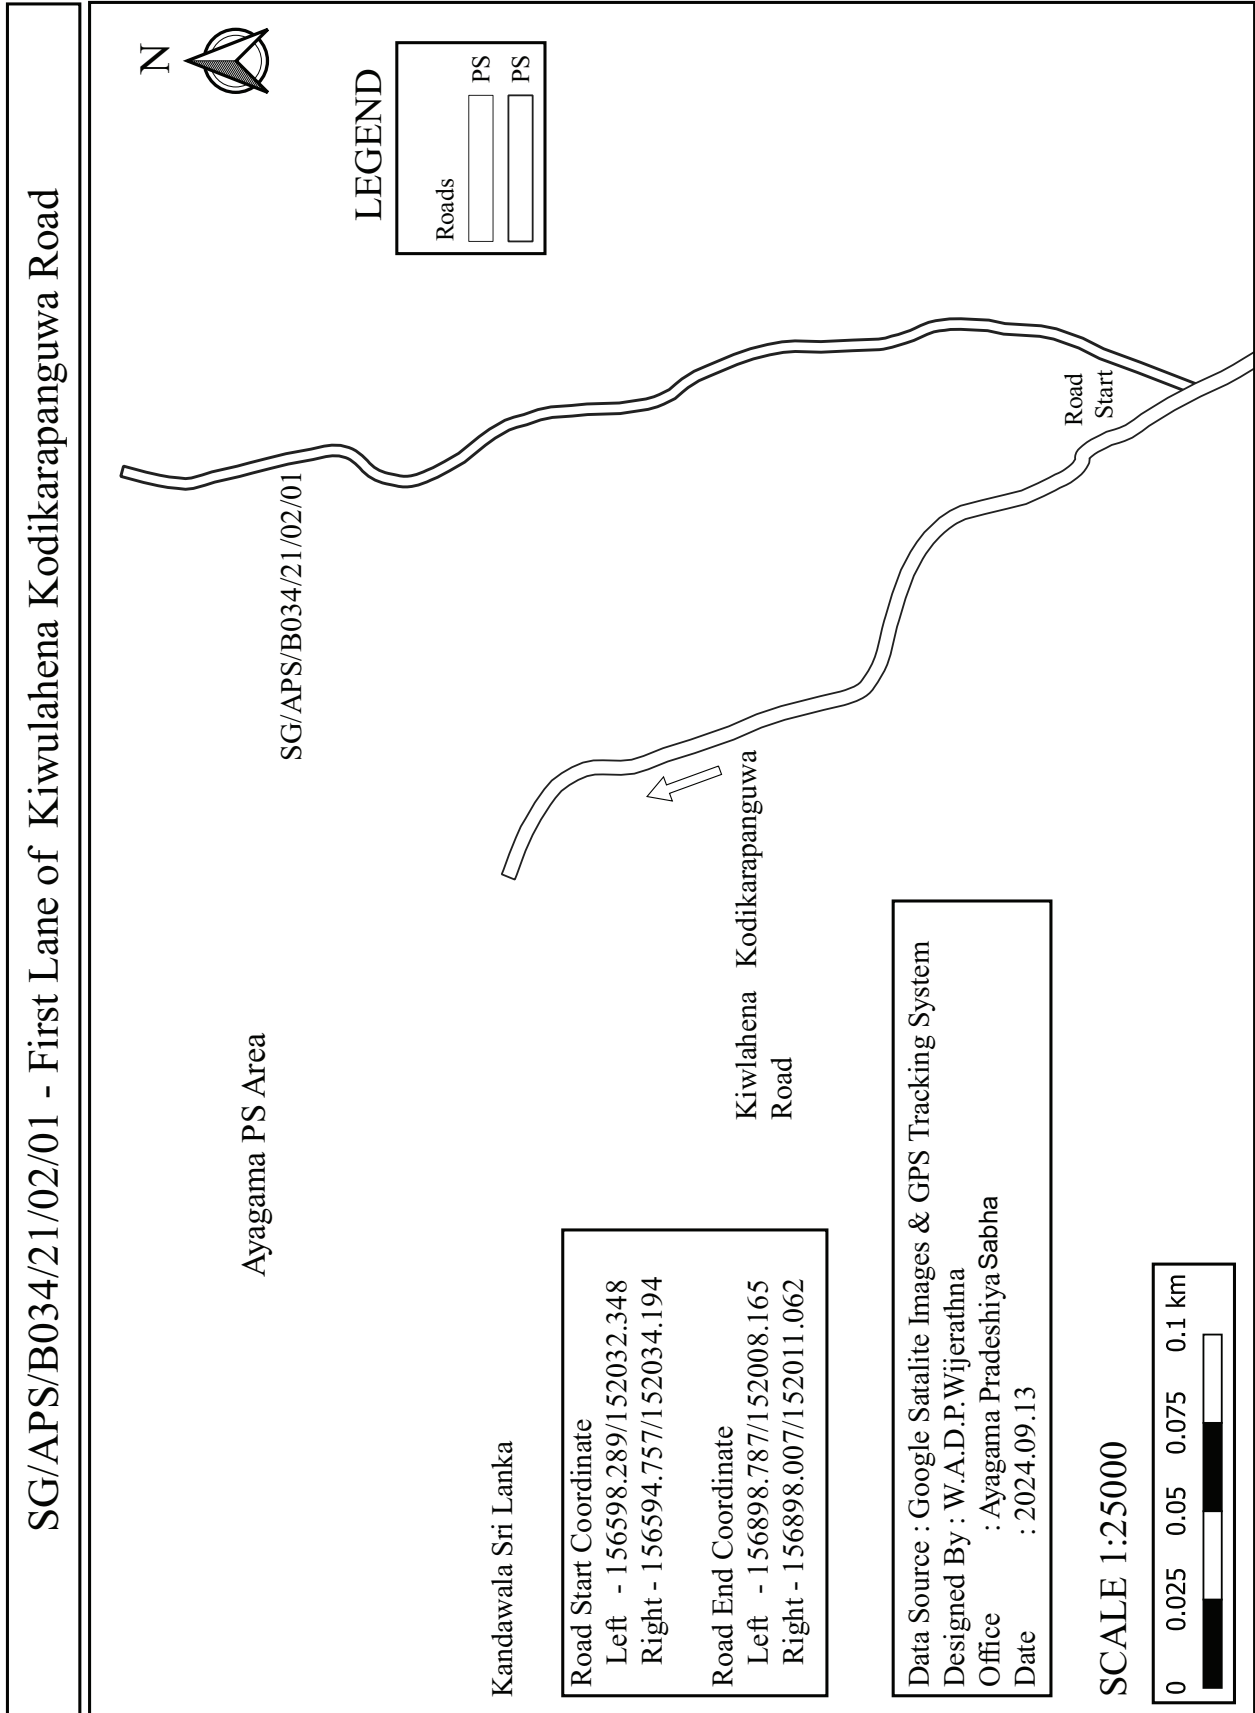


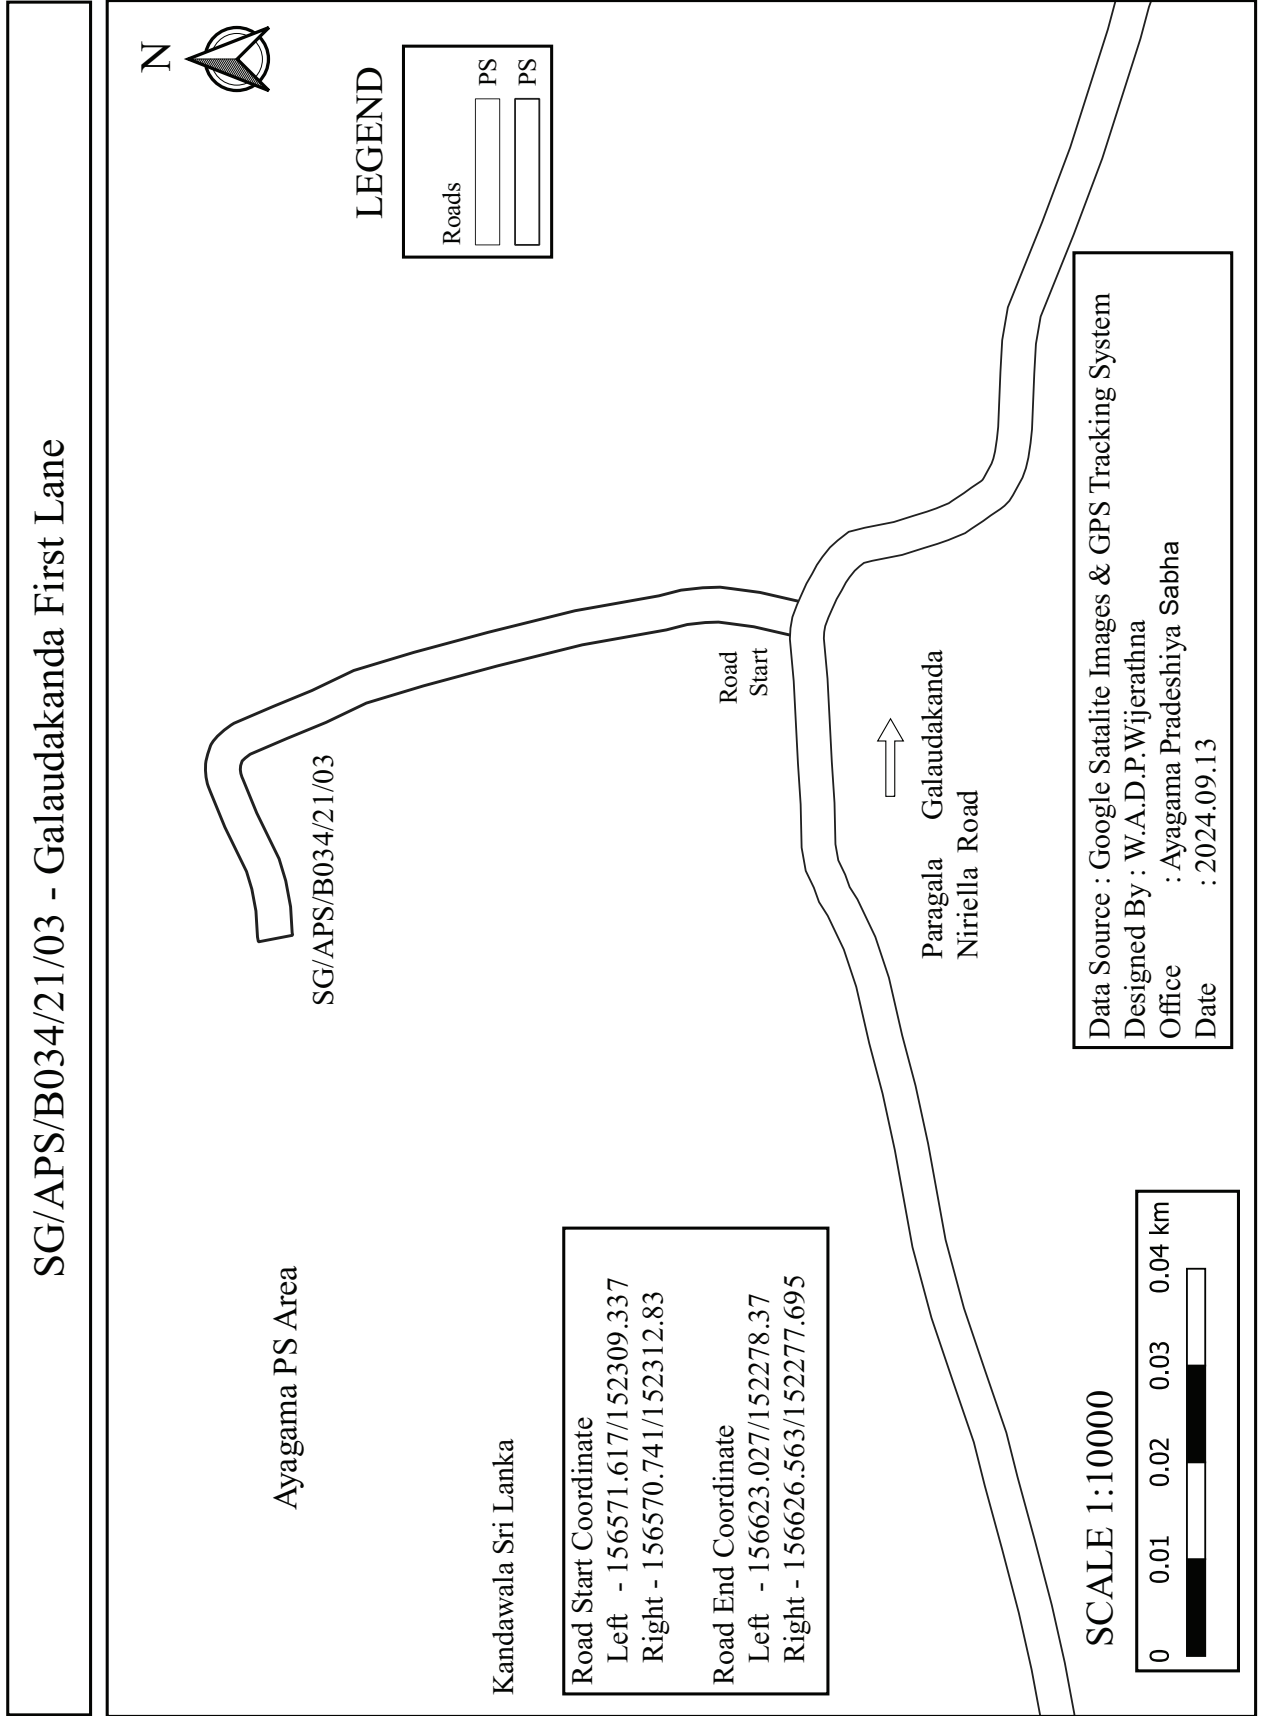


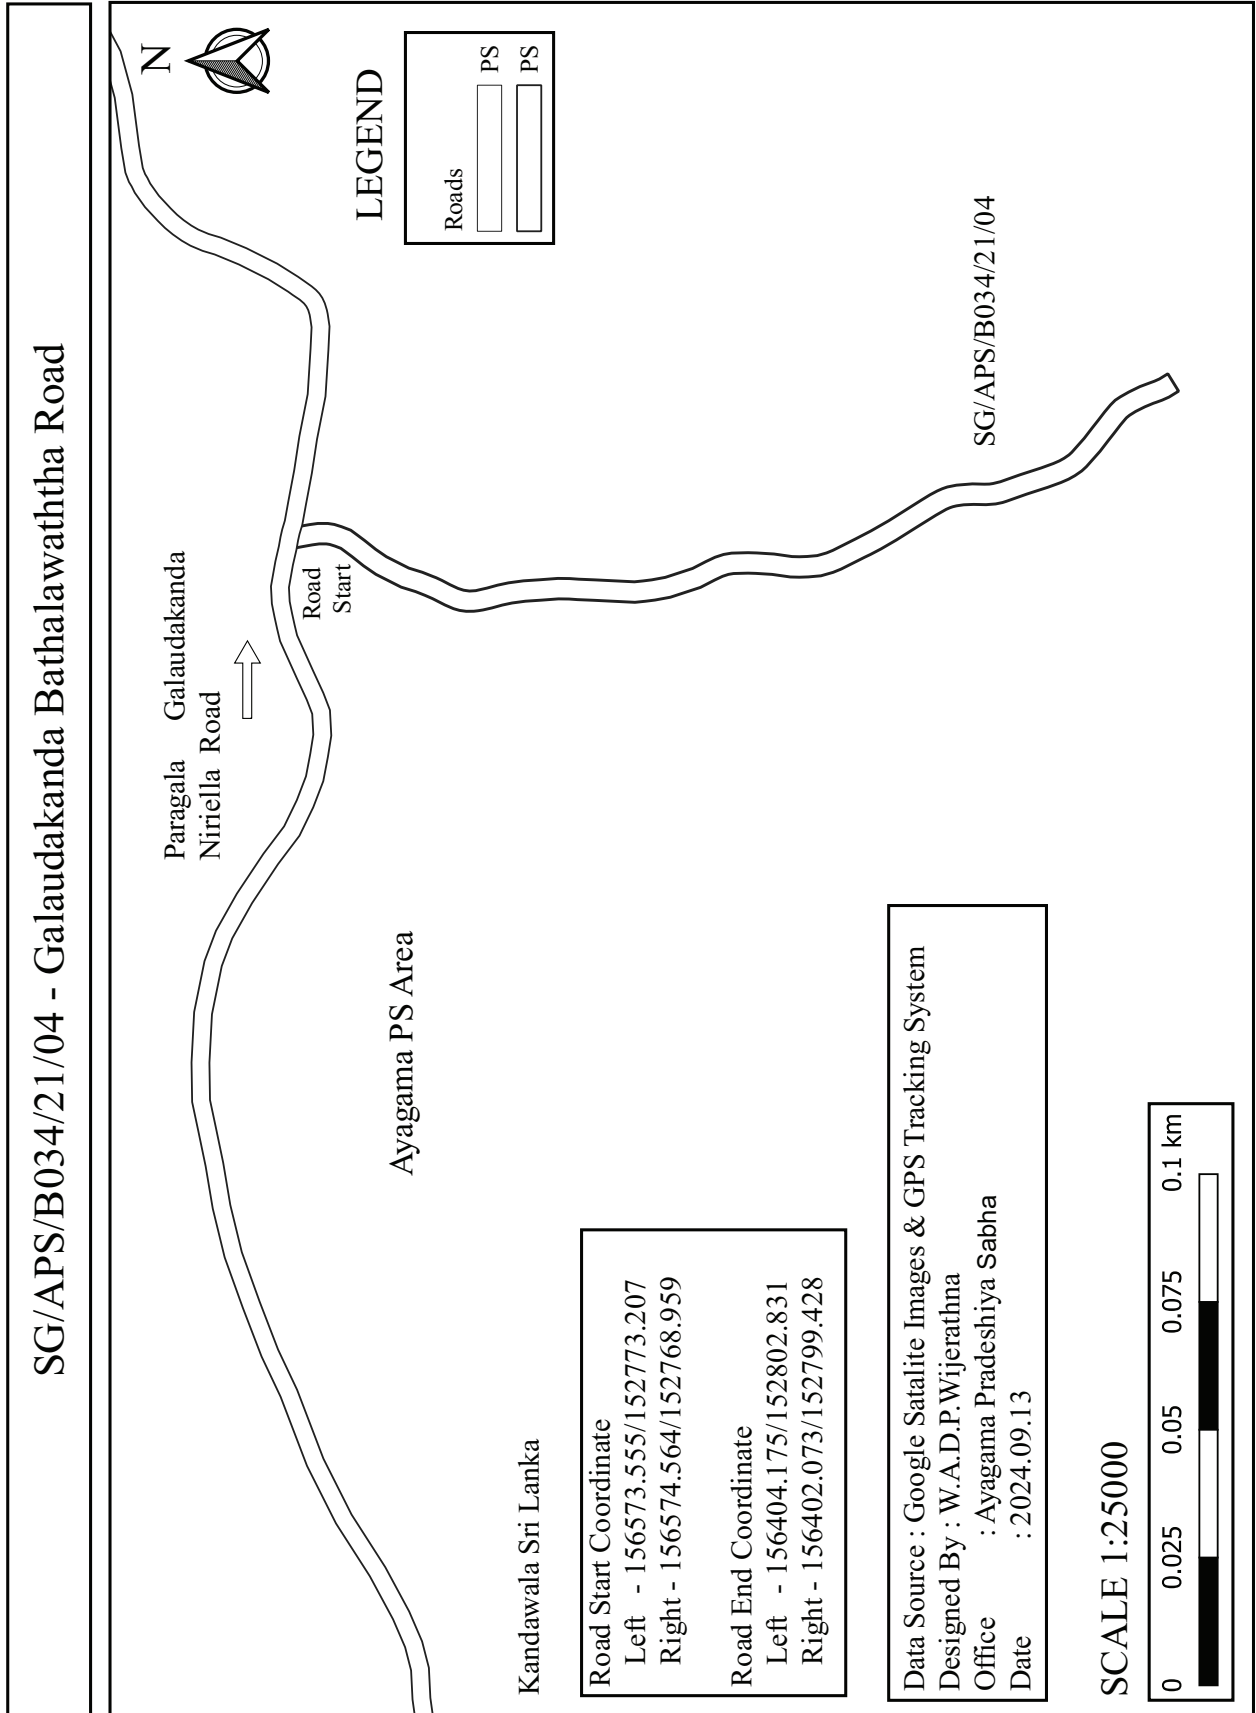


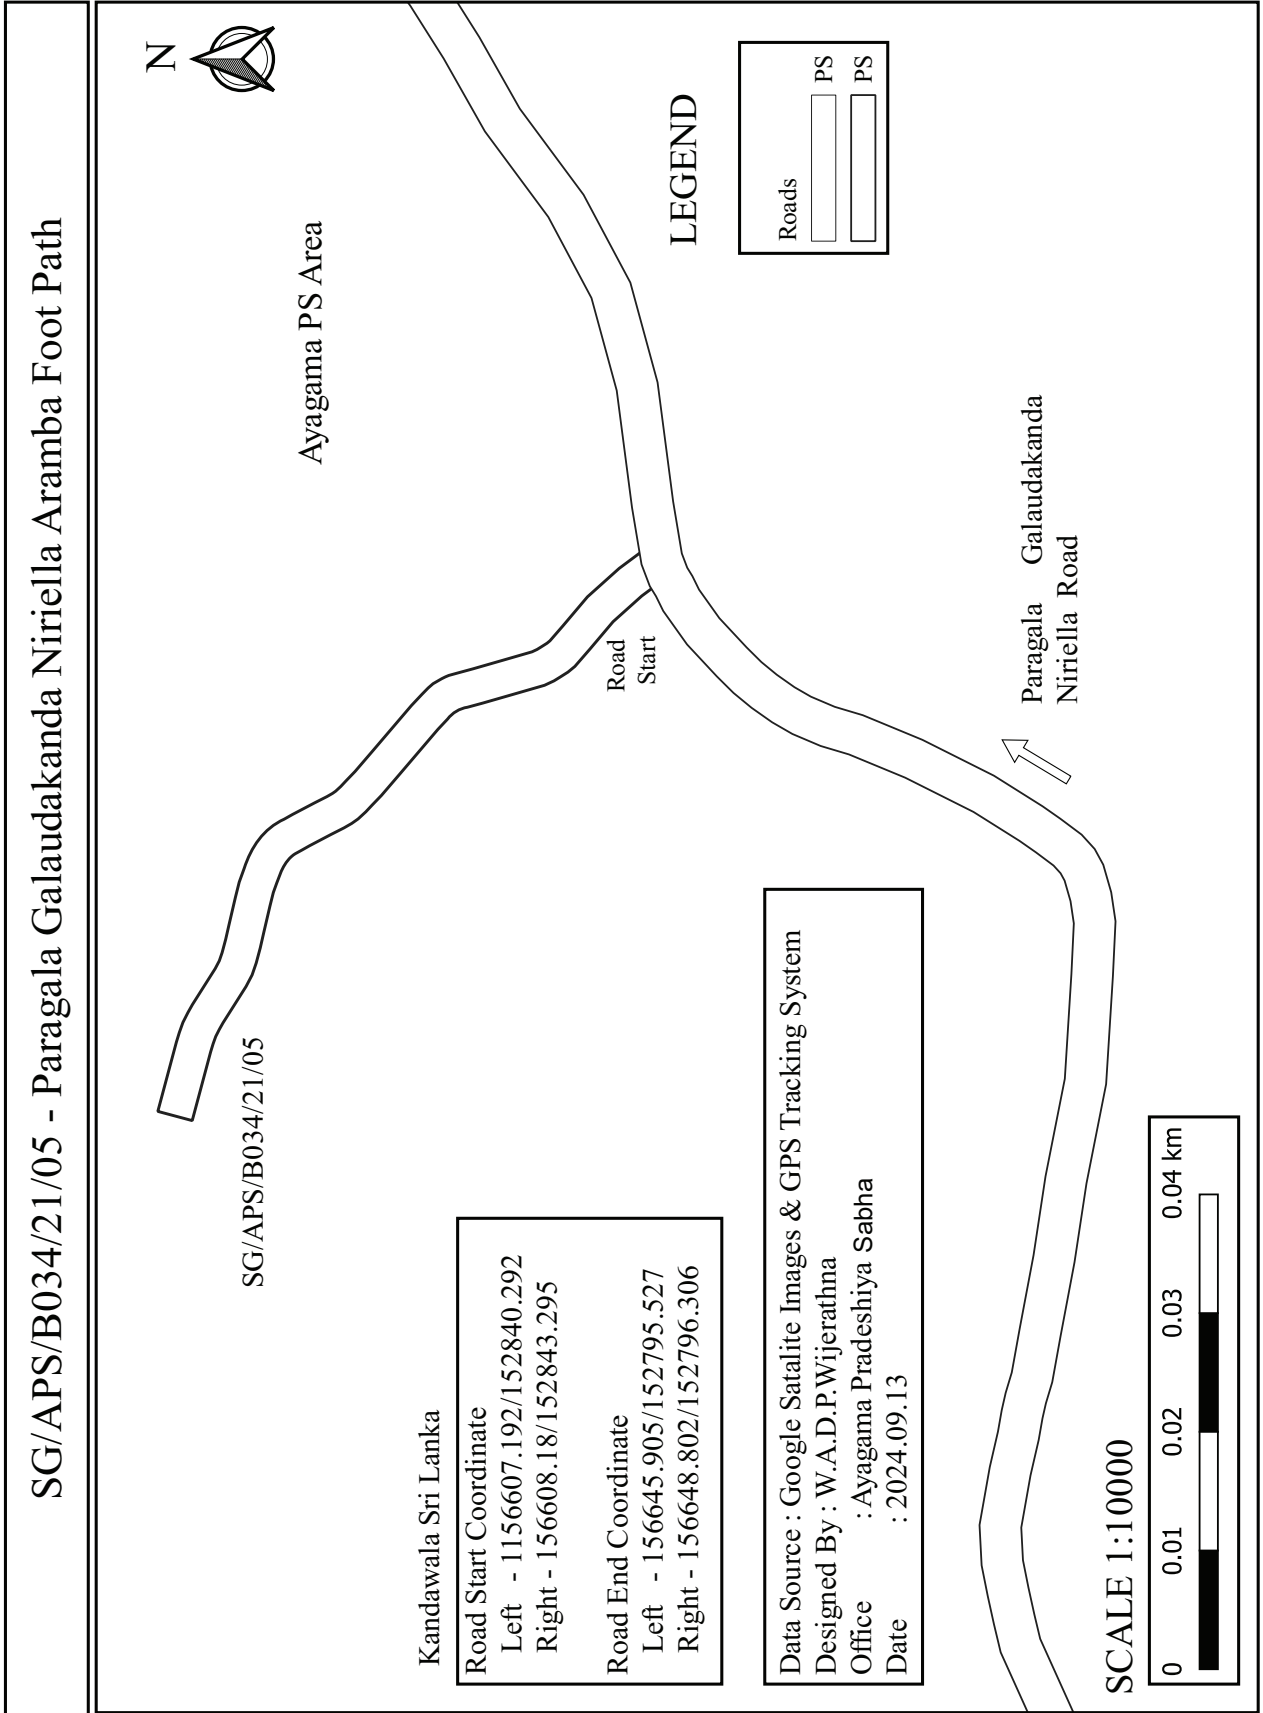


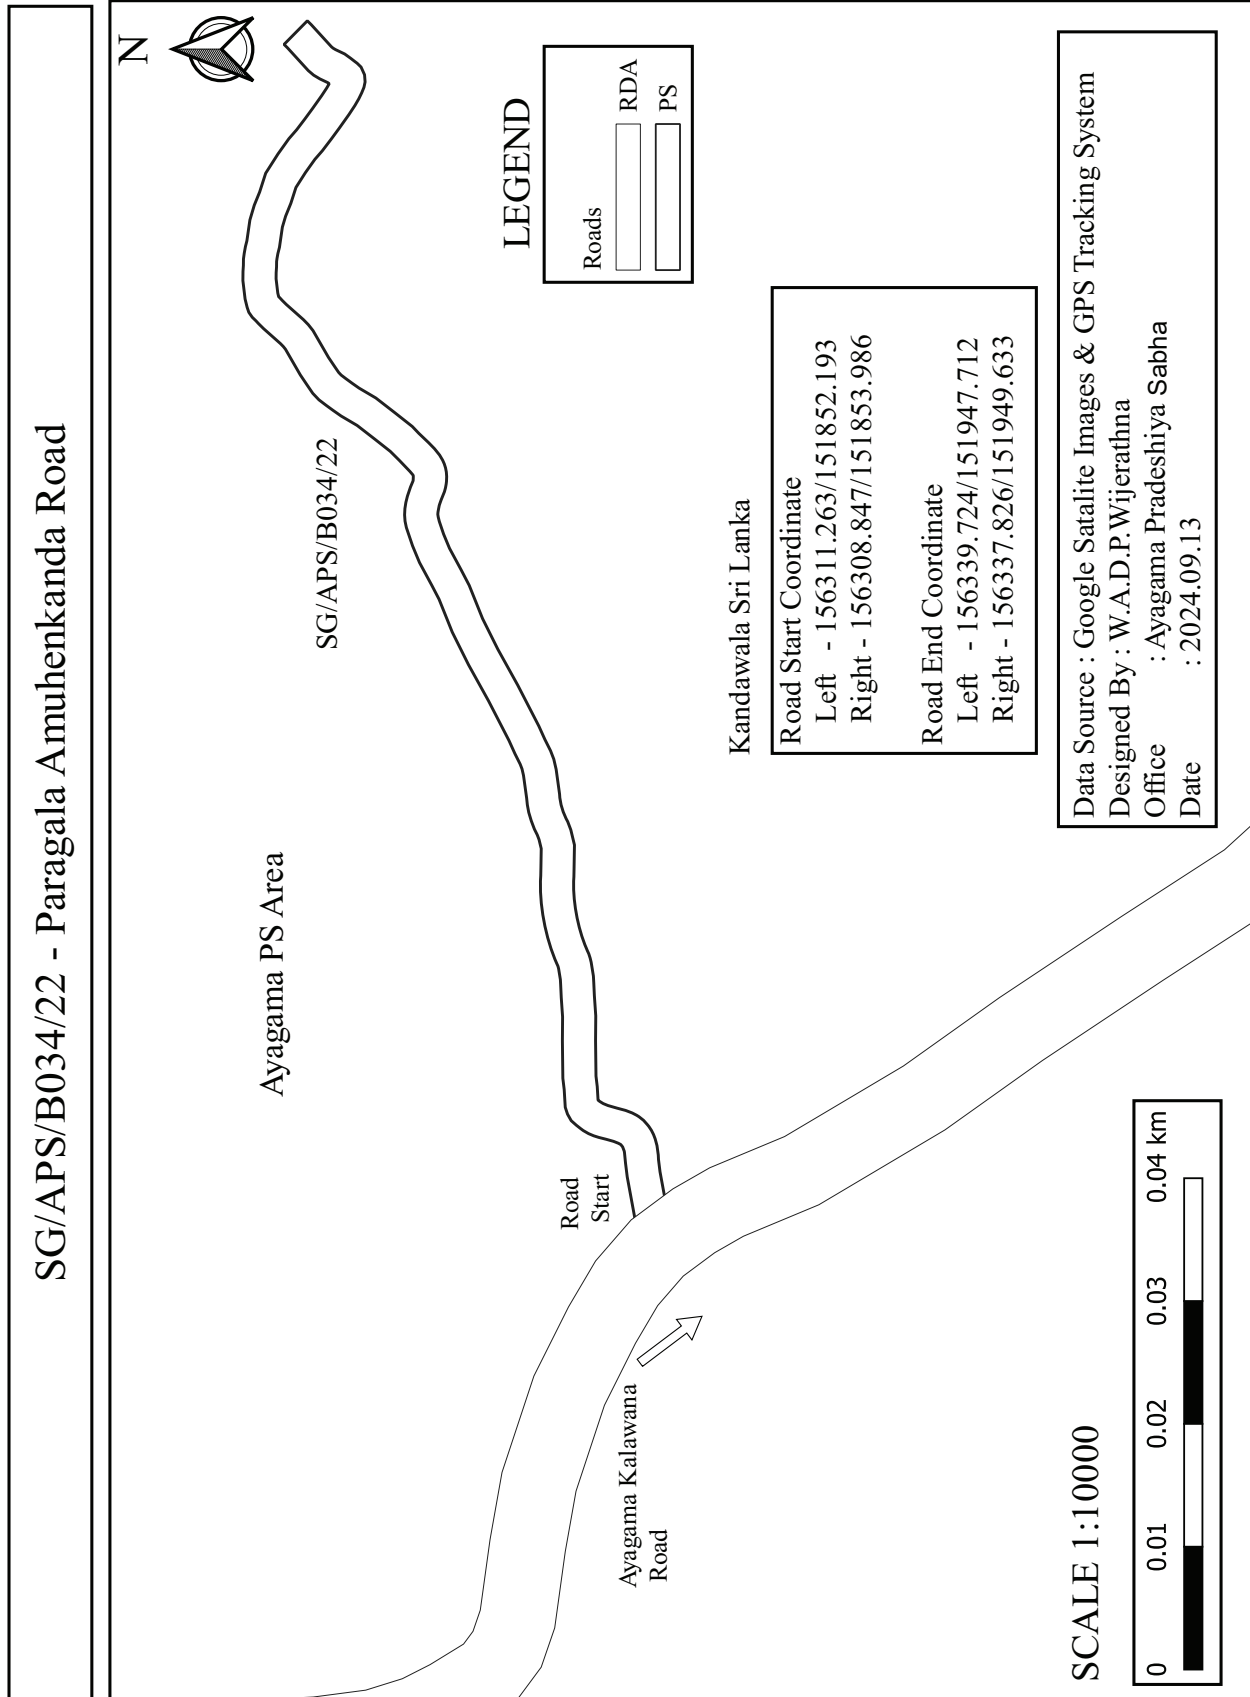


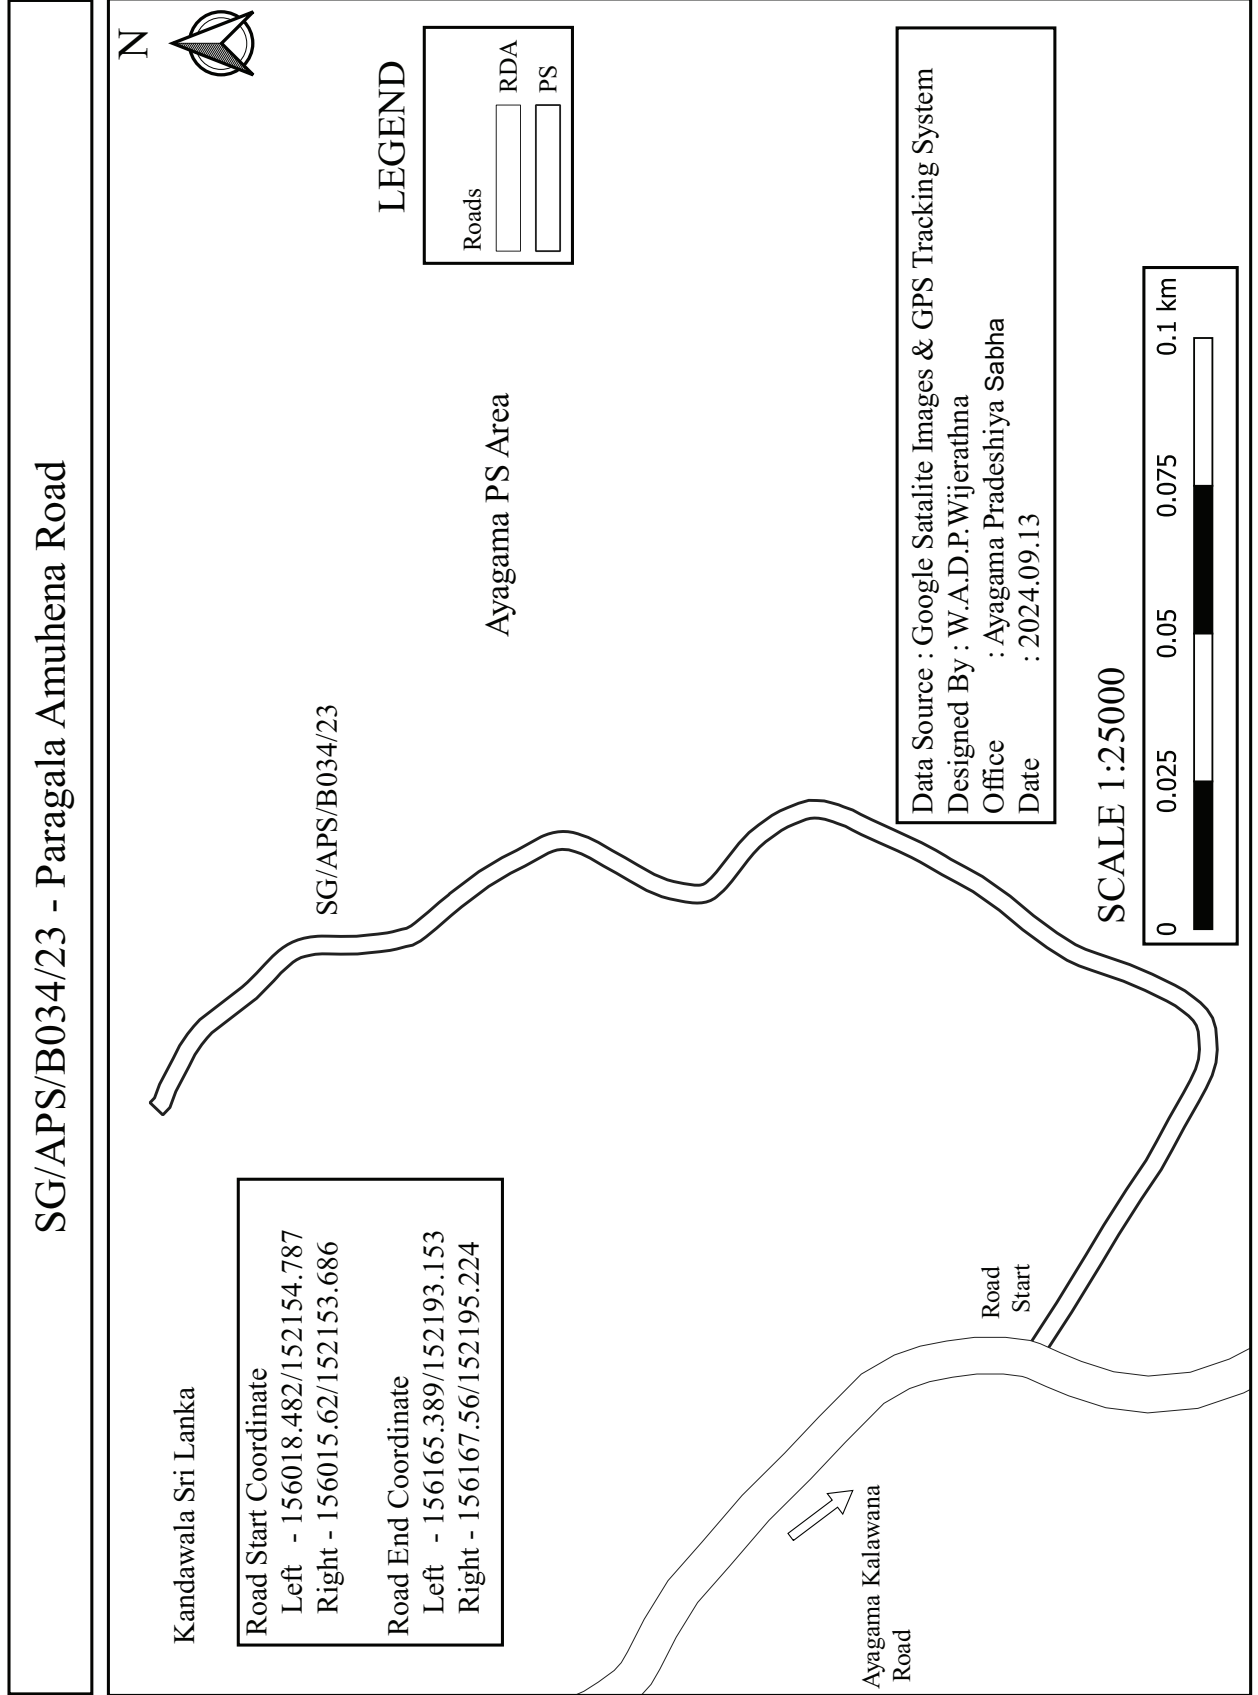

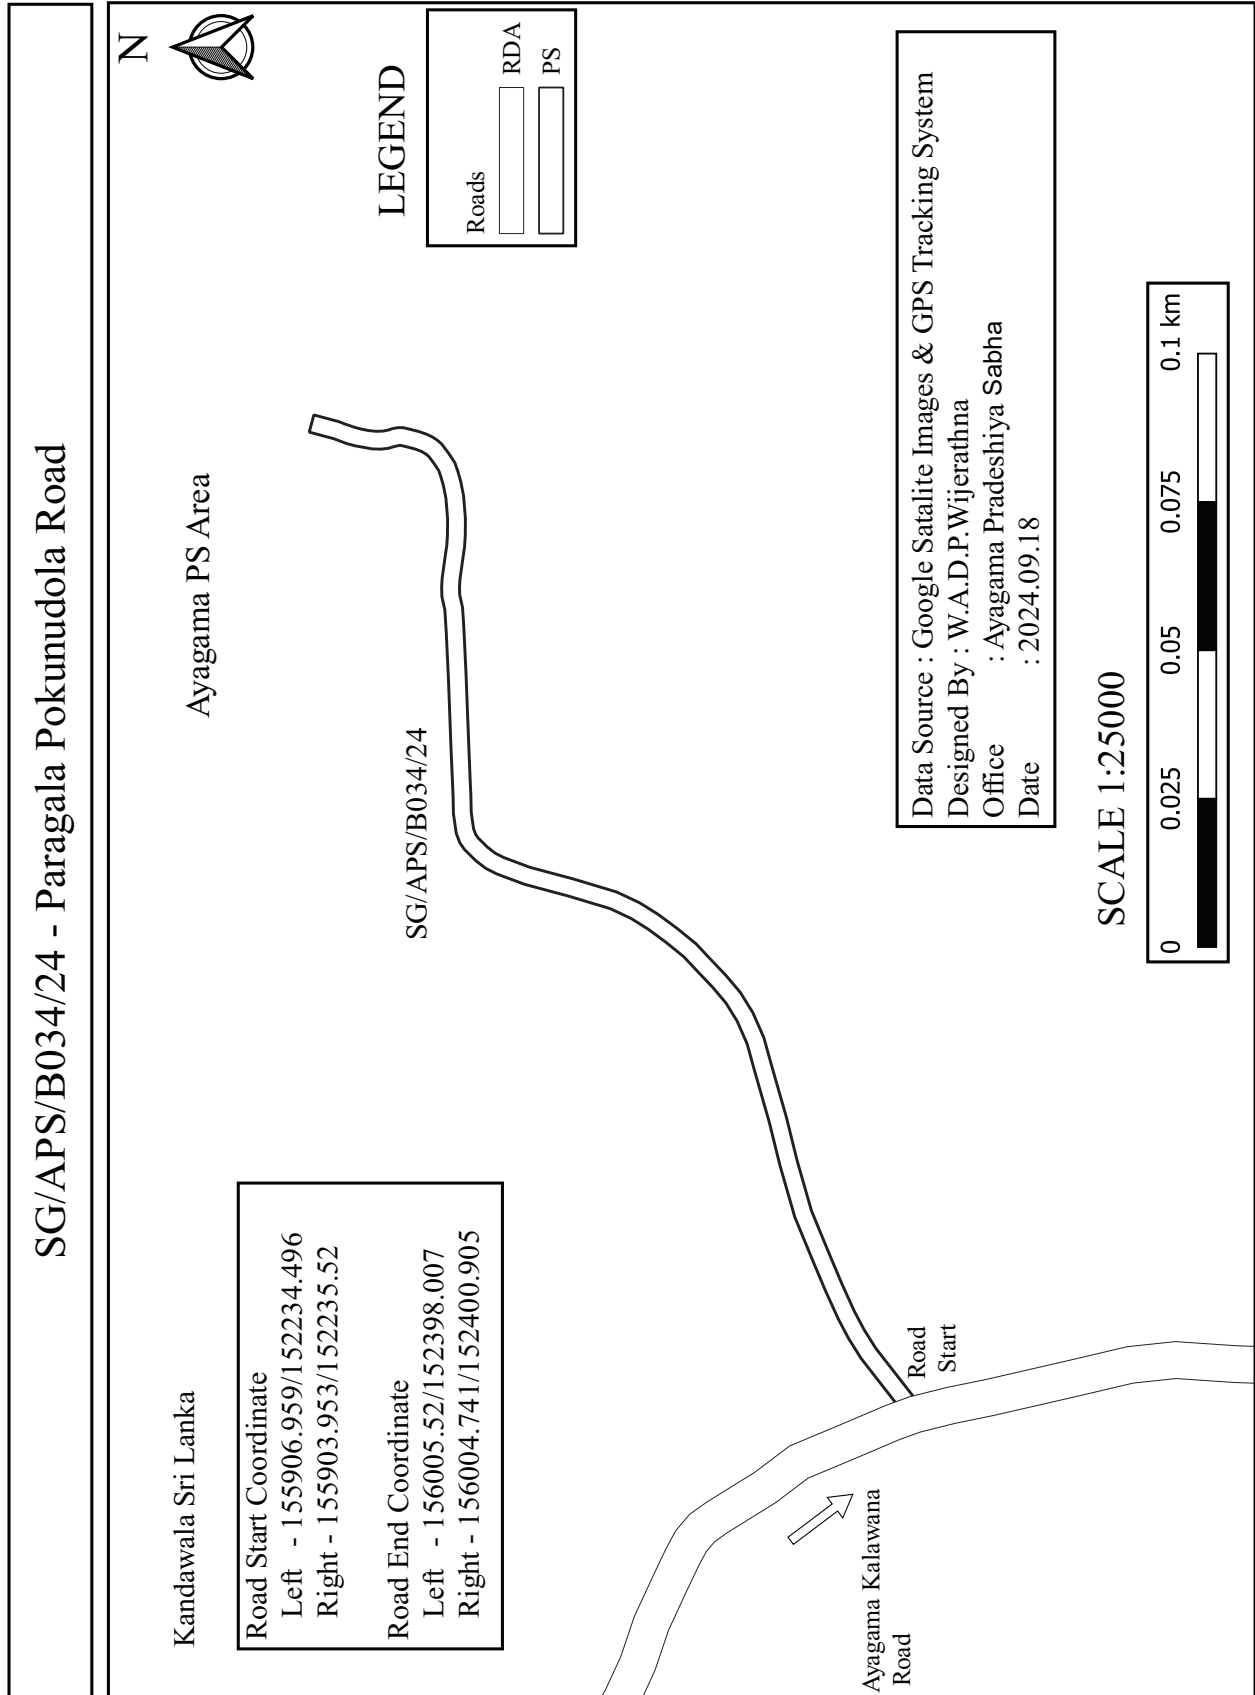


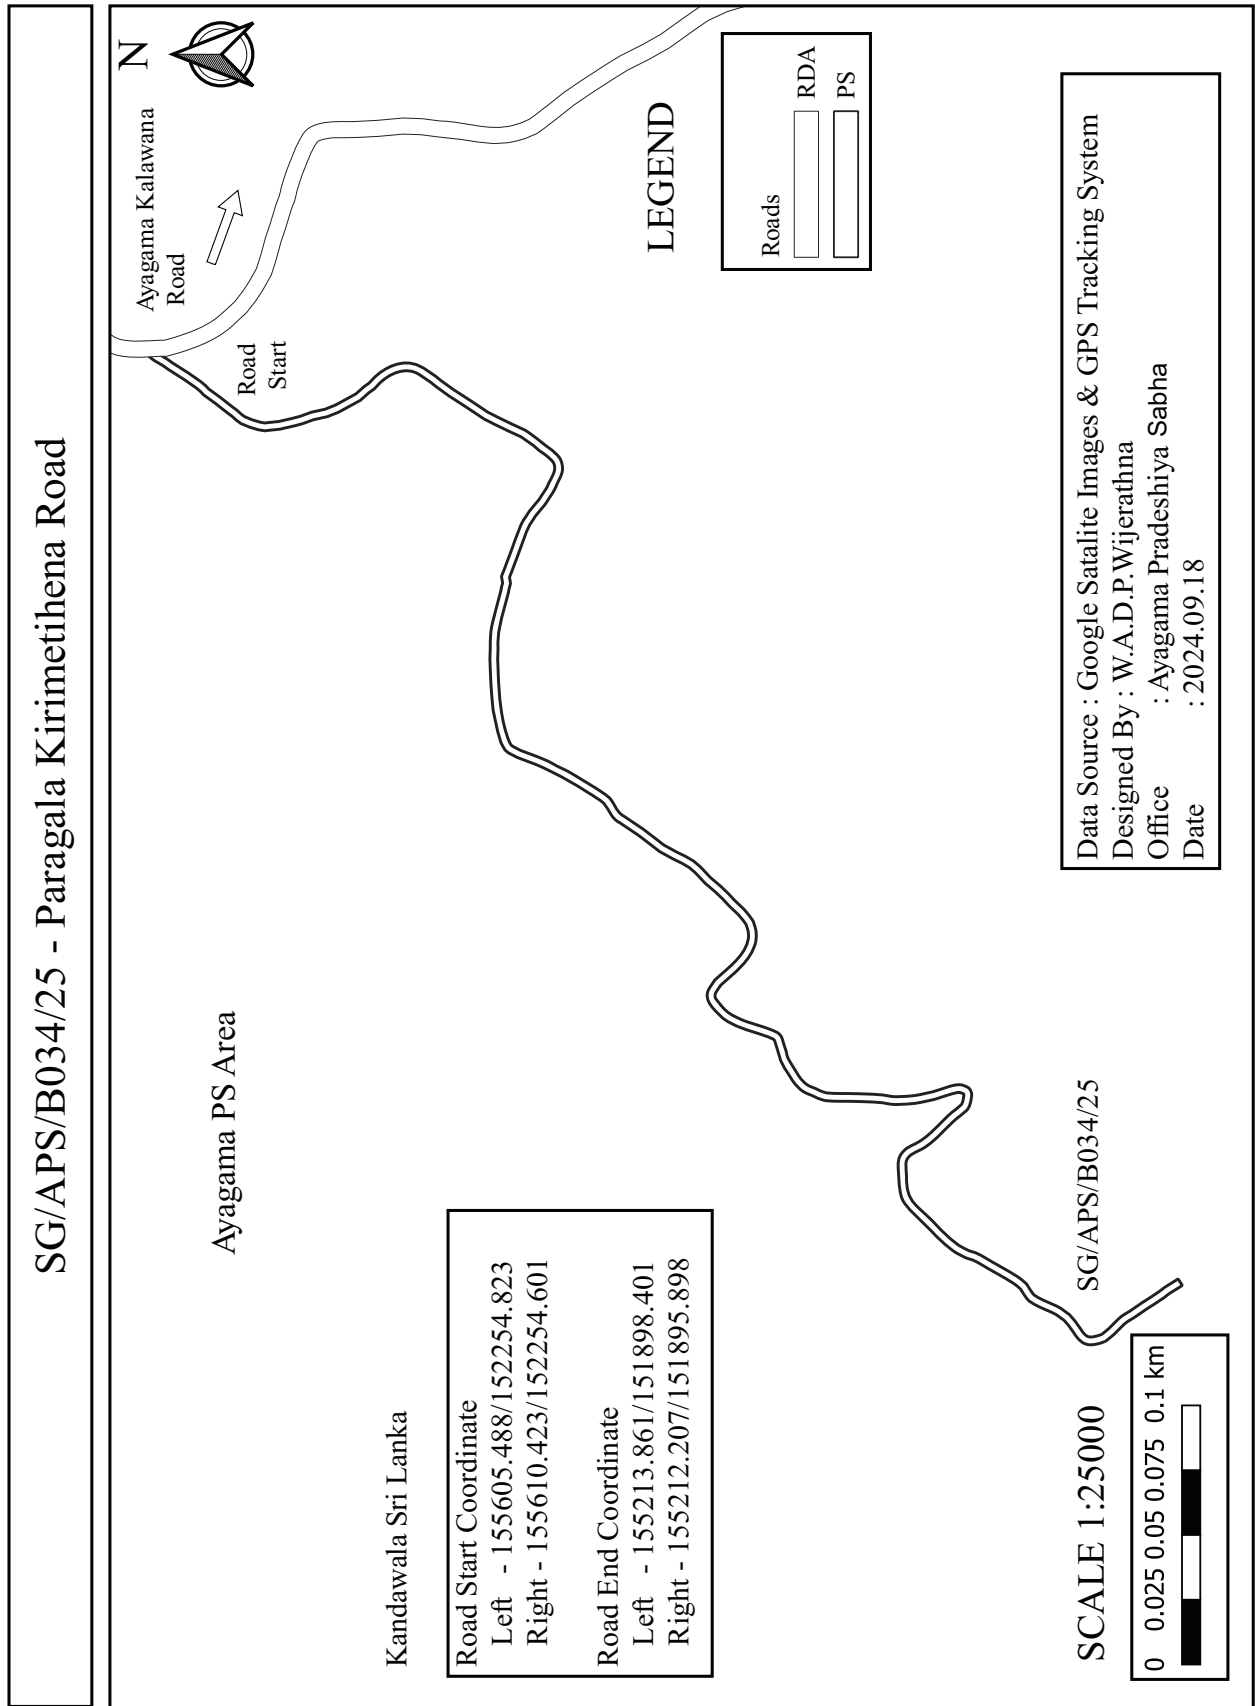


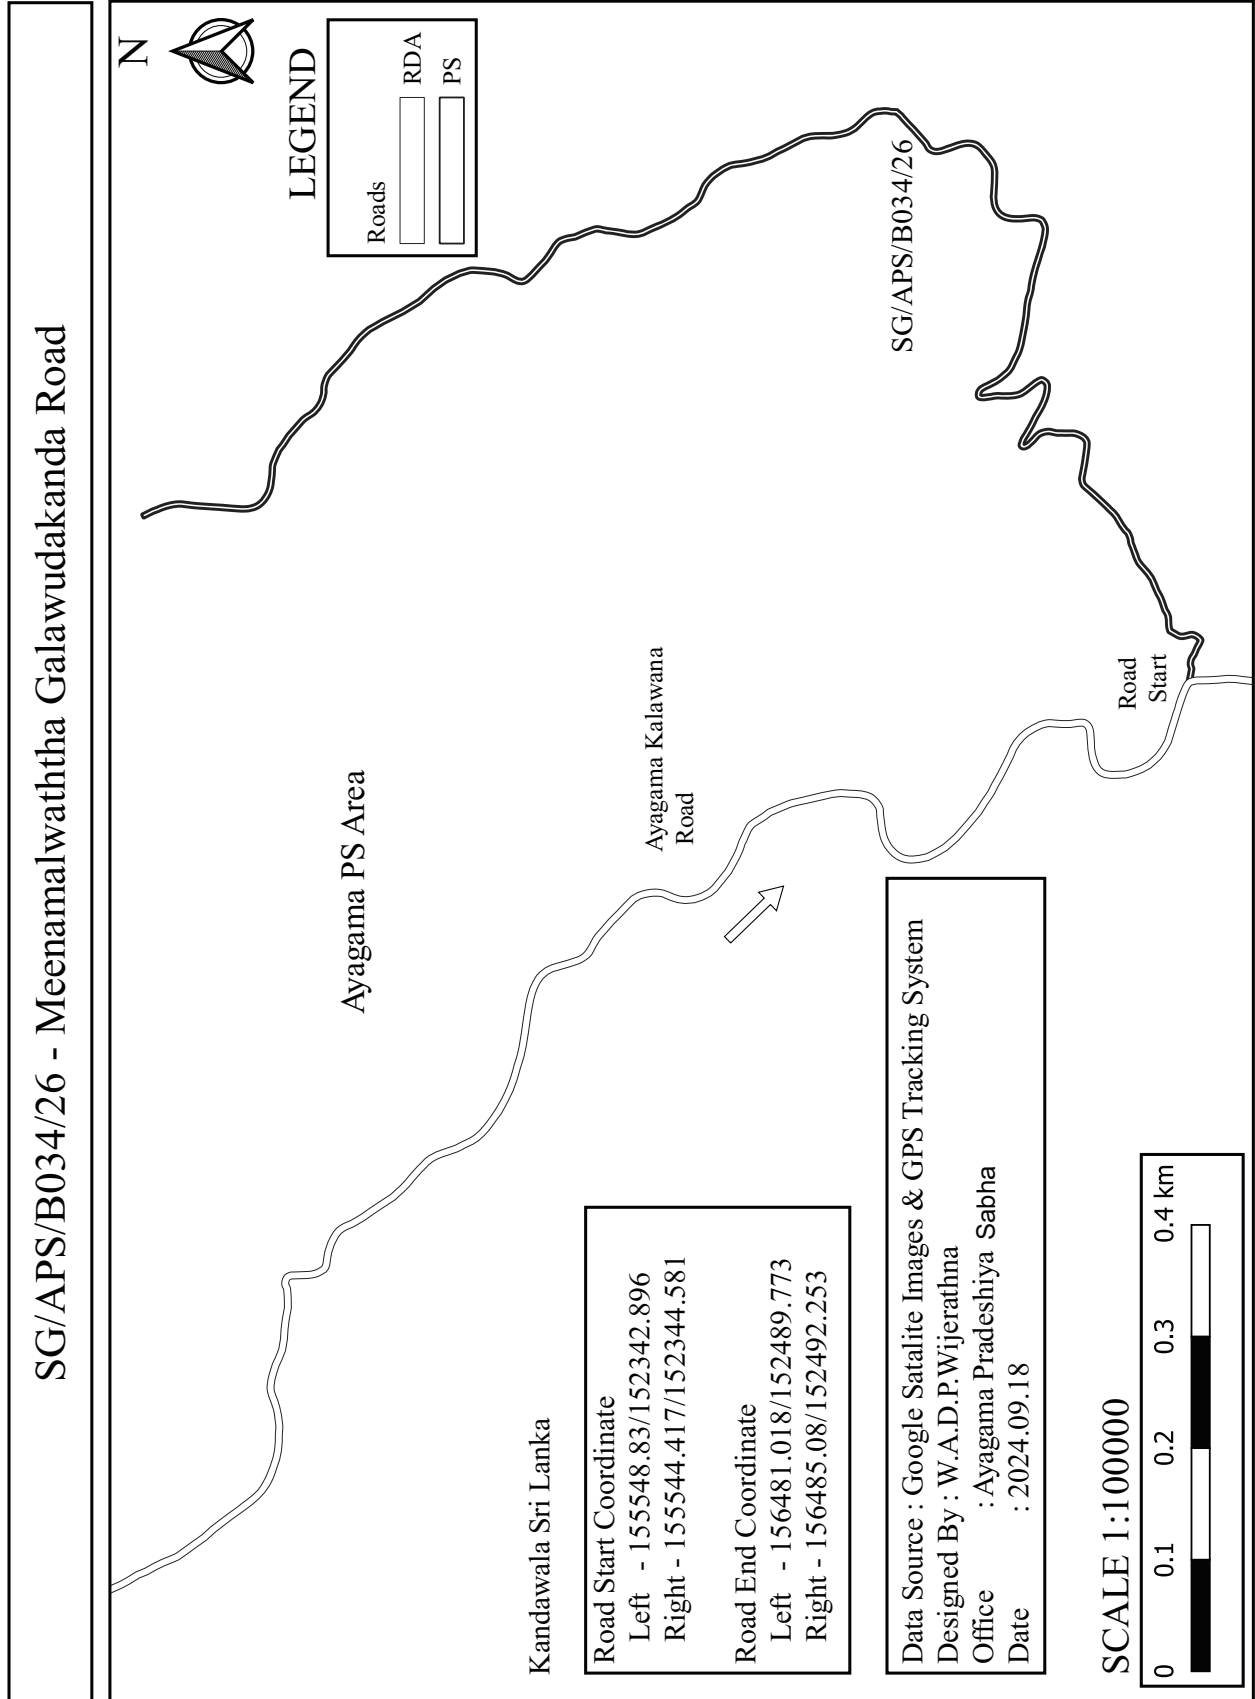


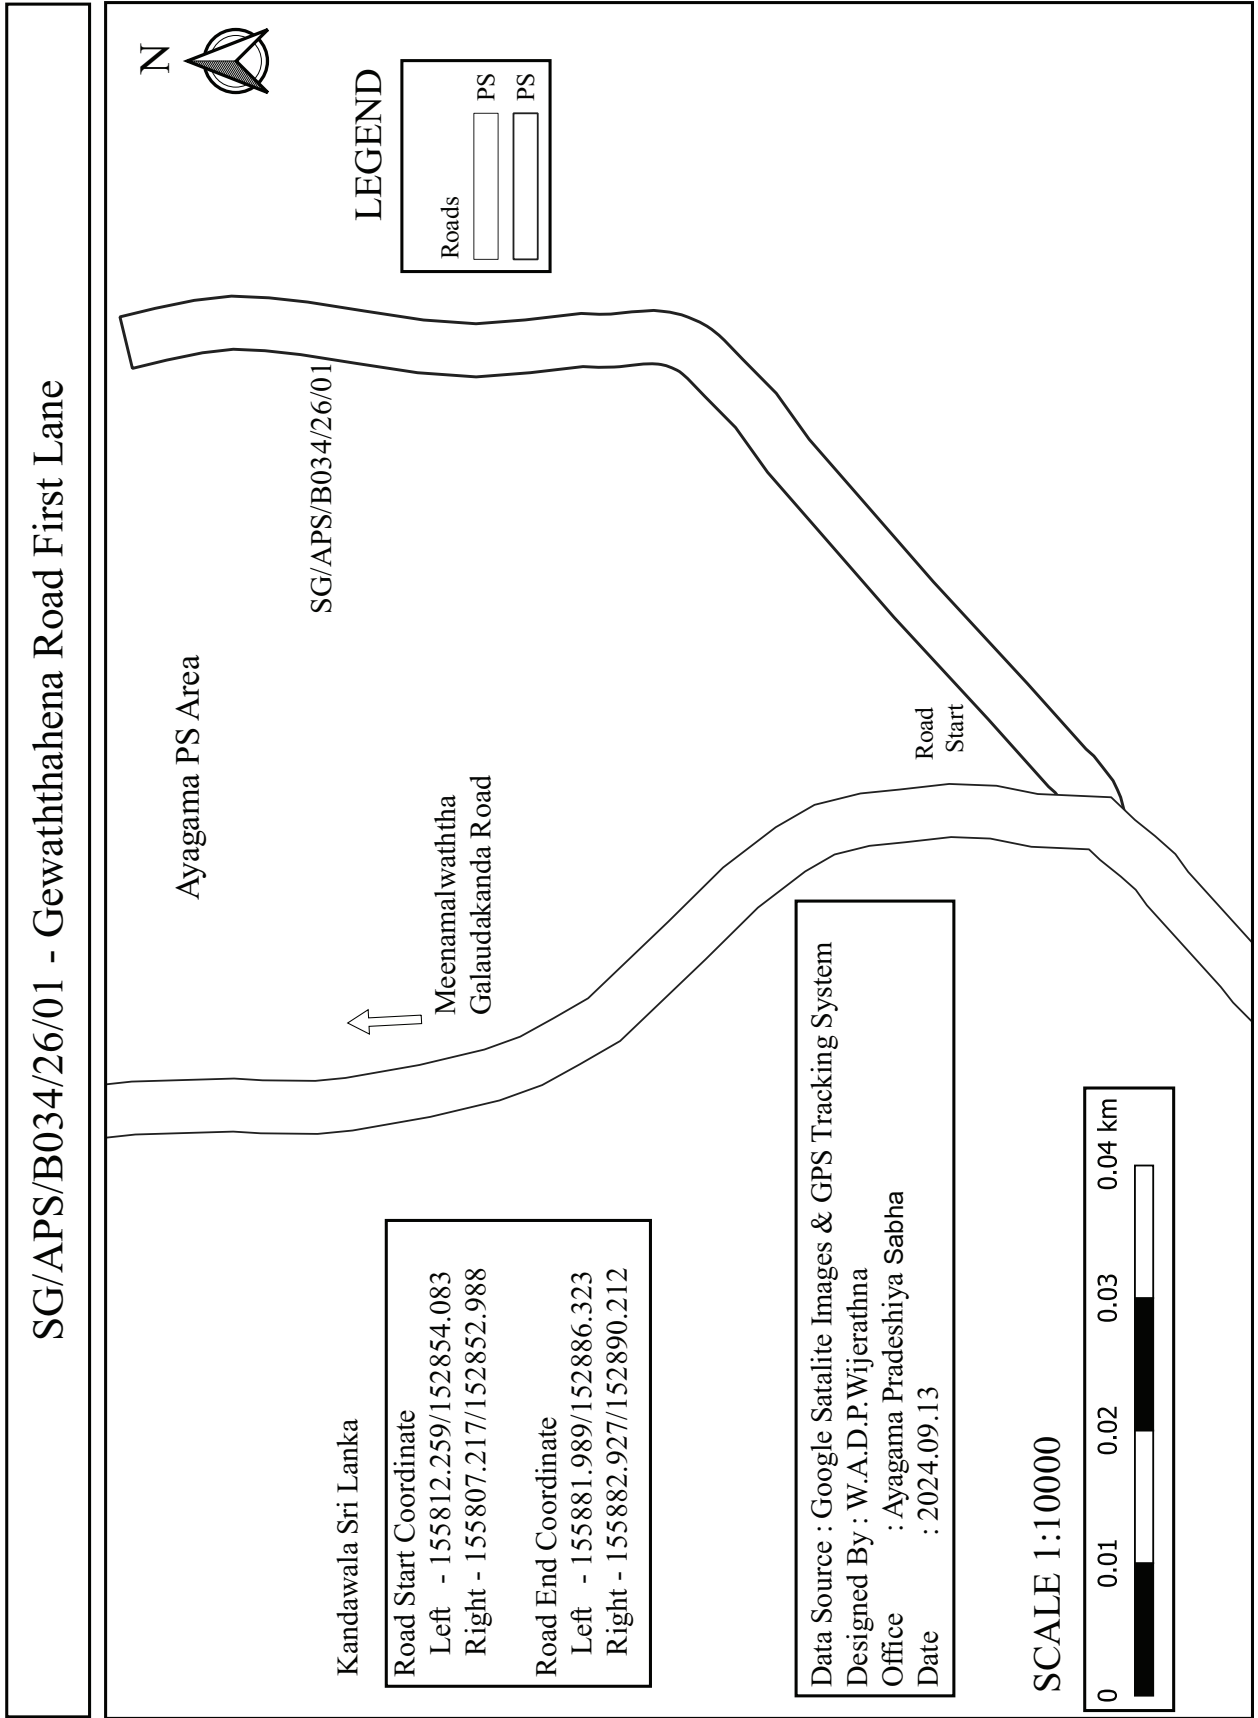

SG/APS/B034/26/02 - Gewaththahena Road Second Lane

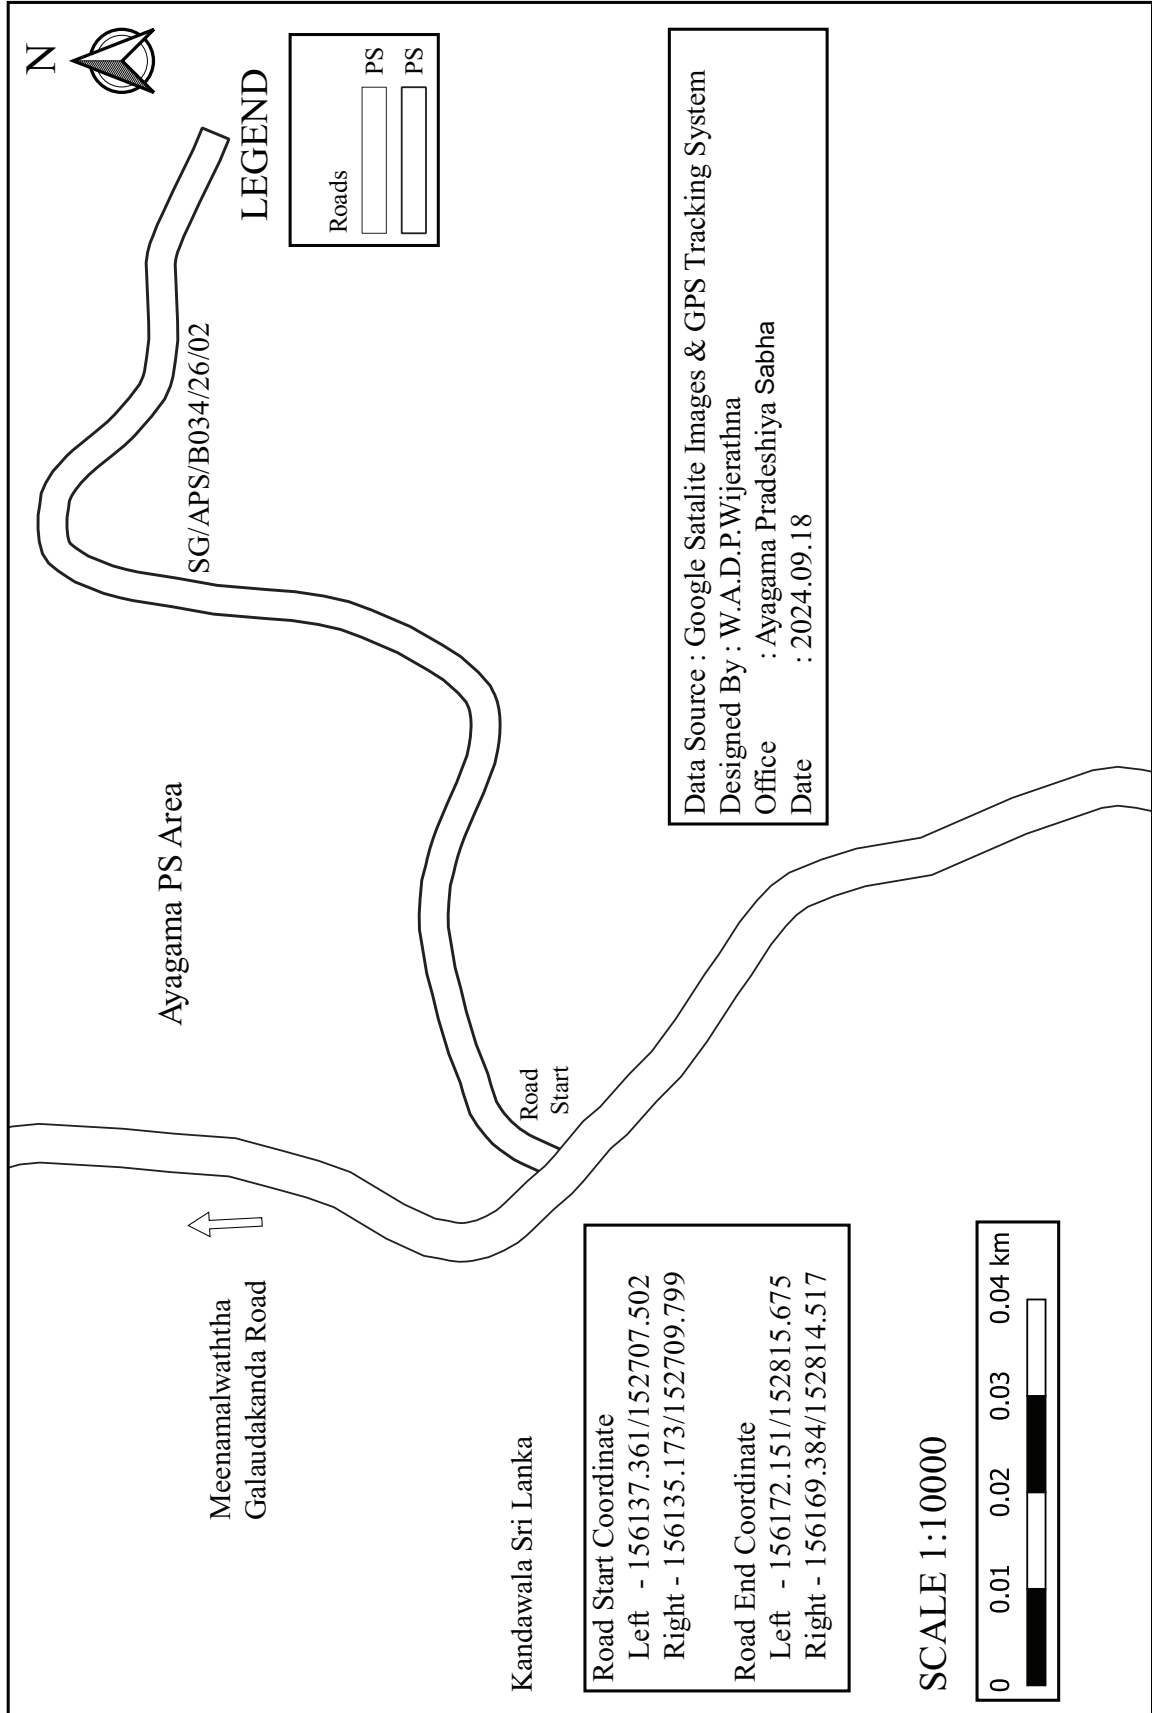

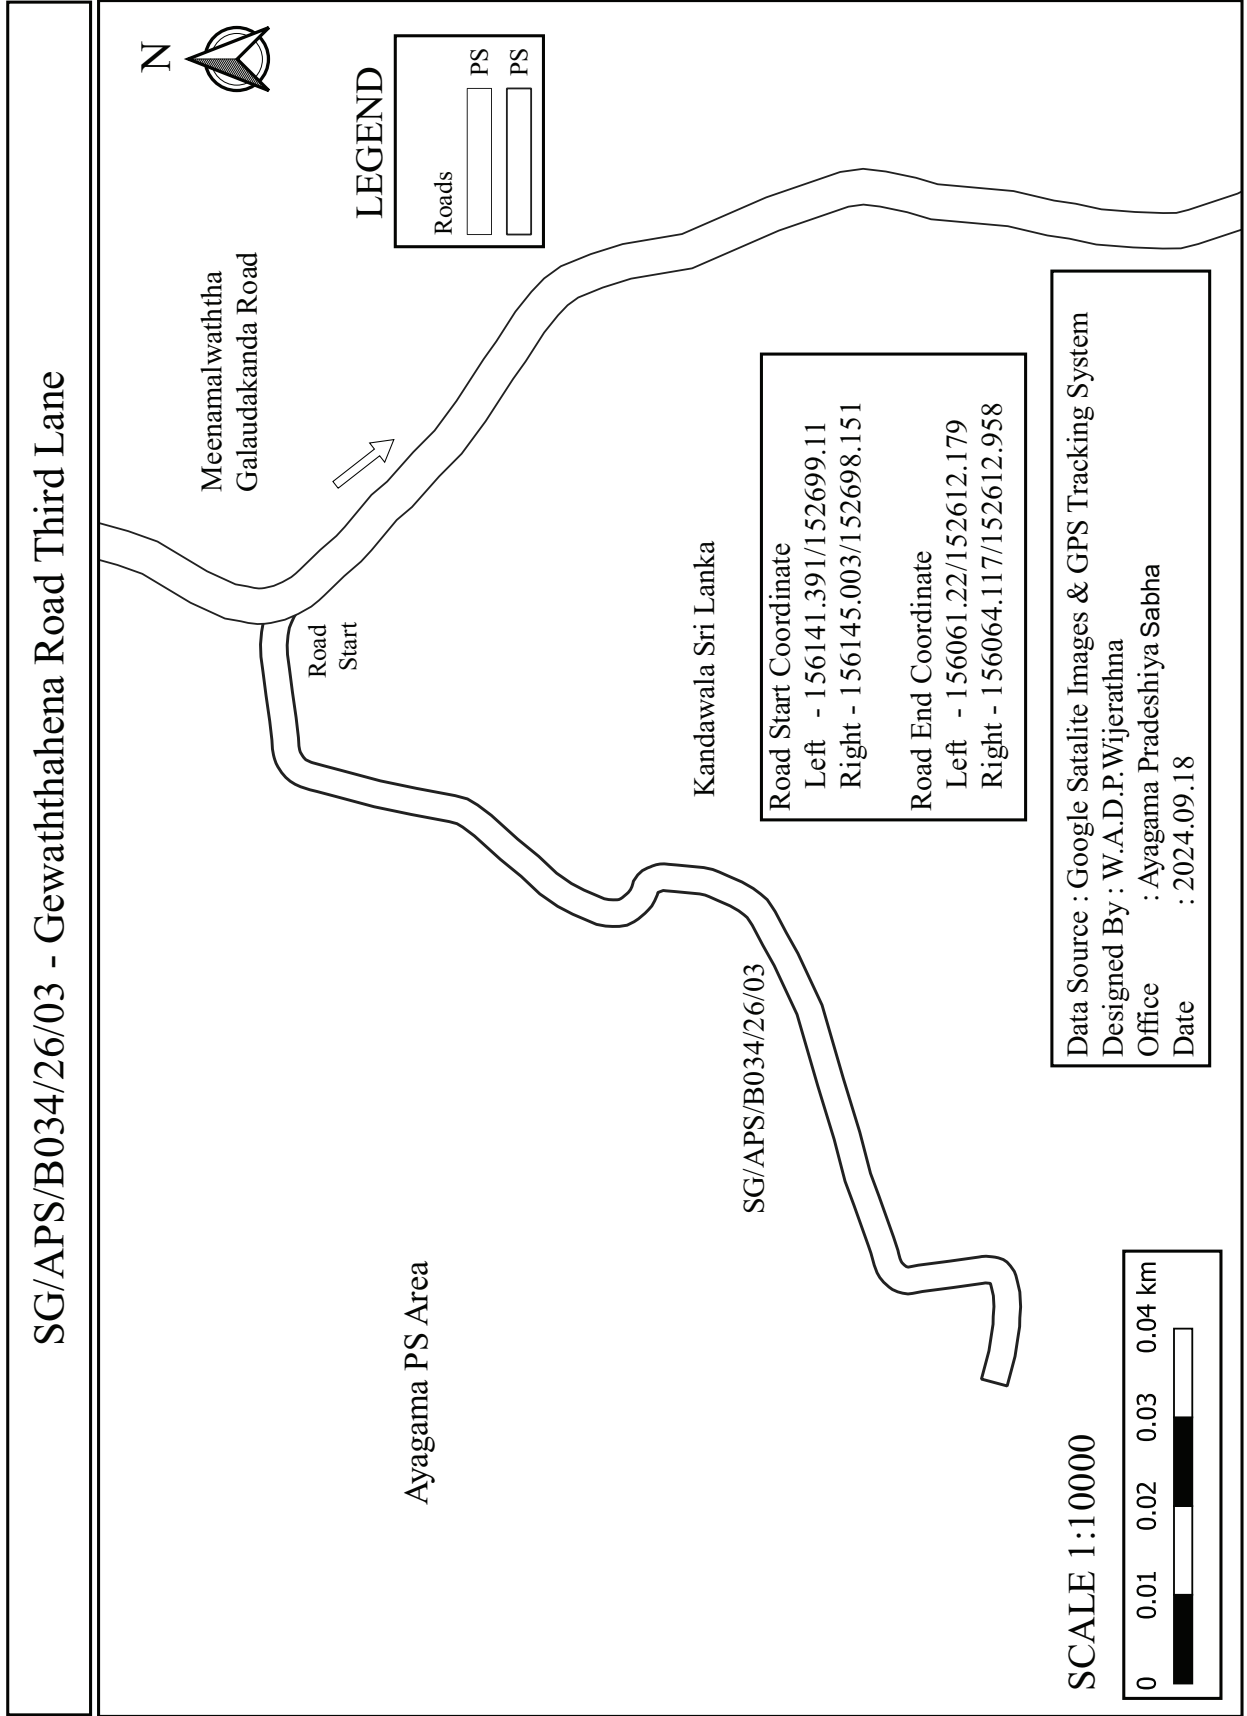

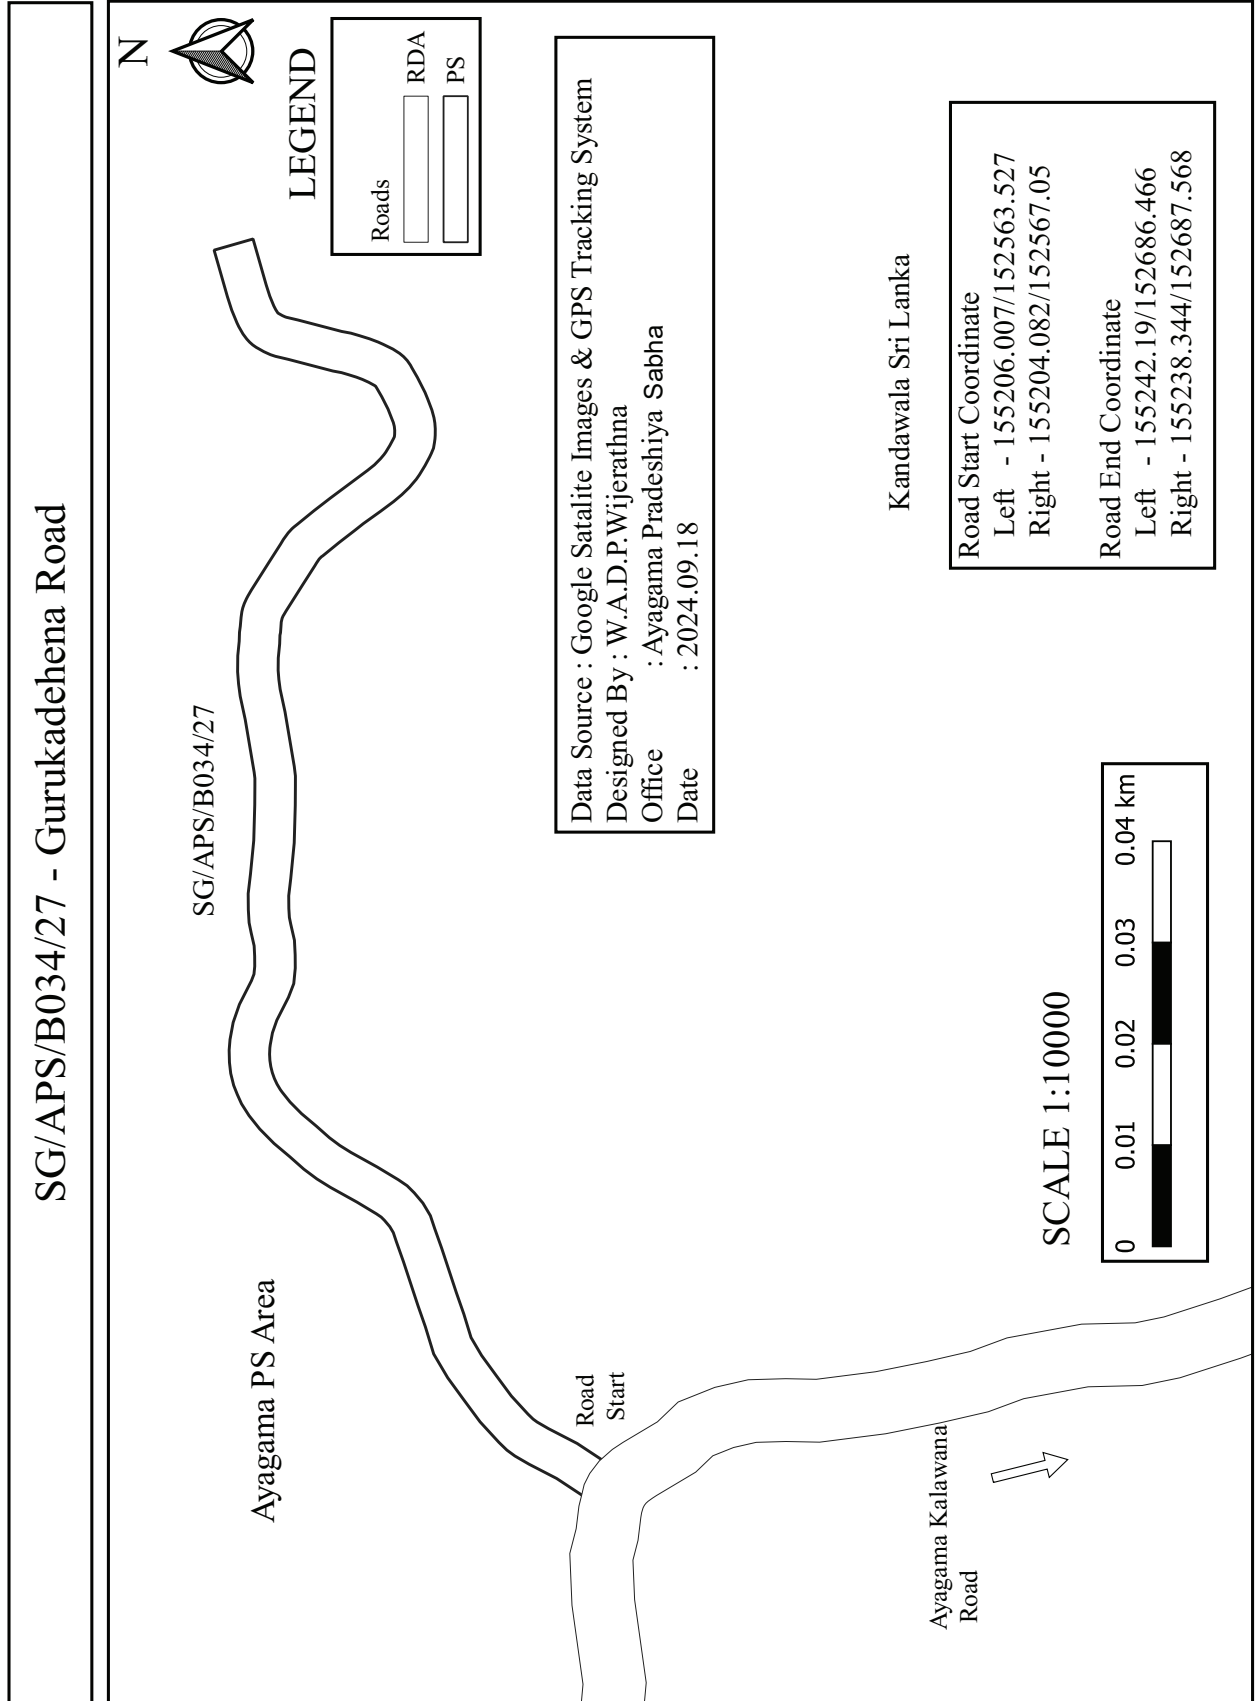


Road Start Coordinate	Left - 154869.536/152691.801
	Right - 154873.824/152690.24
Road End Coordinate	Left - 154751.073/152596.152
	Right - 154754.425/152598.333

Left - 154869.536/152691.801
Right - 154873.824/152690.24

Road End Coordinate
Left - 154751.073/152596.152
Right - 154754.425/152598.333

SG/APS/B034/28

SCALE 1:25000

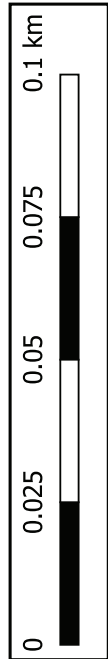

Data Source : Google Satalite Images & GPS Tracking System
Designed By : W.A.D.P.Wijerathna
Office : Ayagama Pradeshiya Sabha
Date : 2024.09.18

Ayagama PS Area


Ayagama Kalawana
Road


LEGEND


Roads


RDA


DC

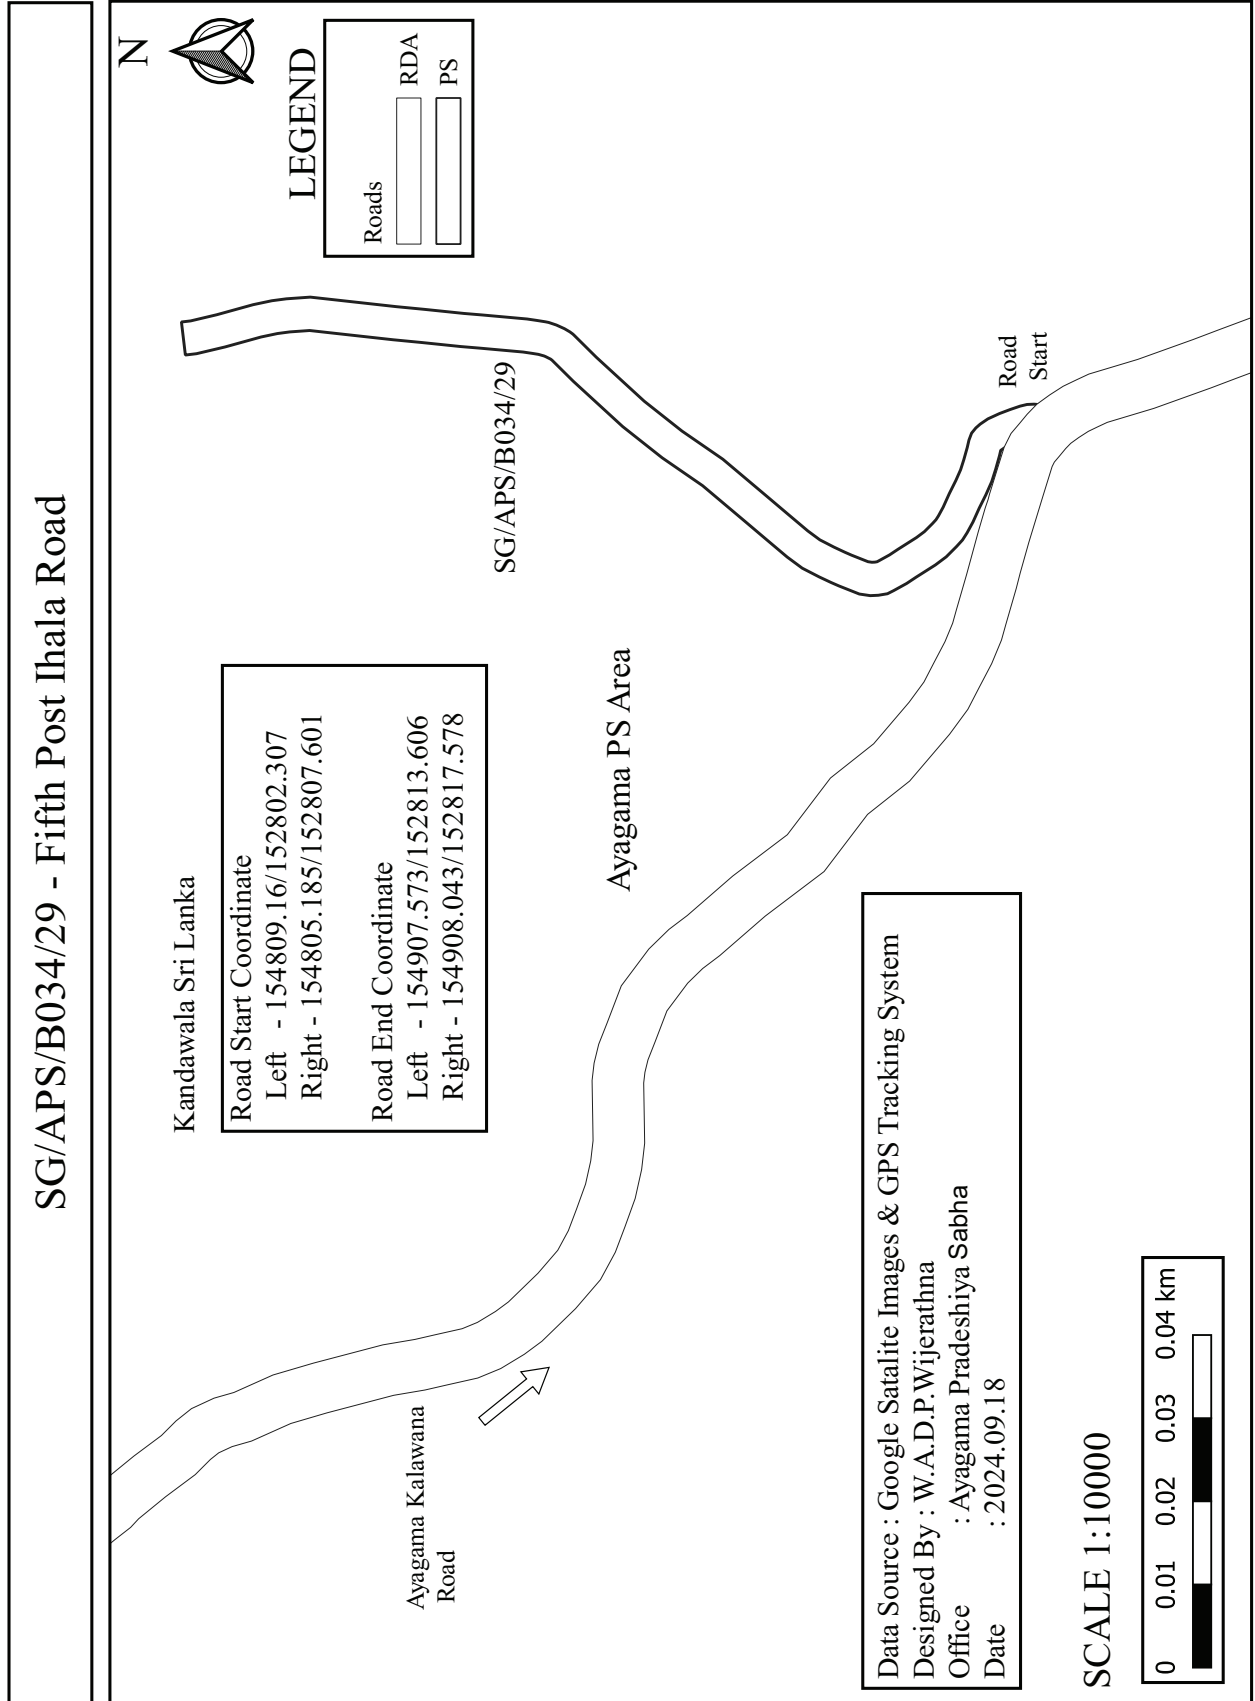


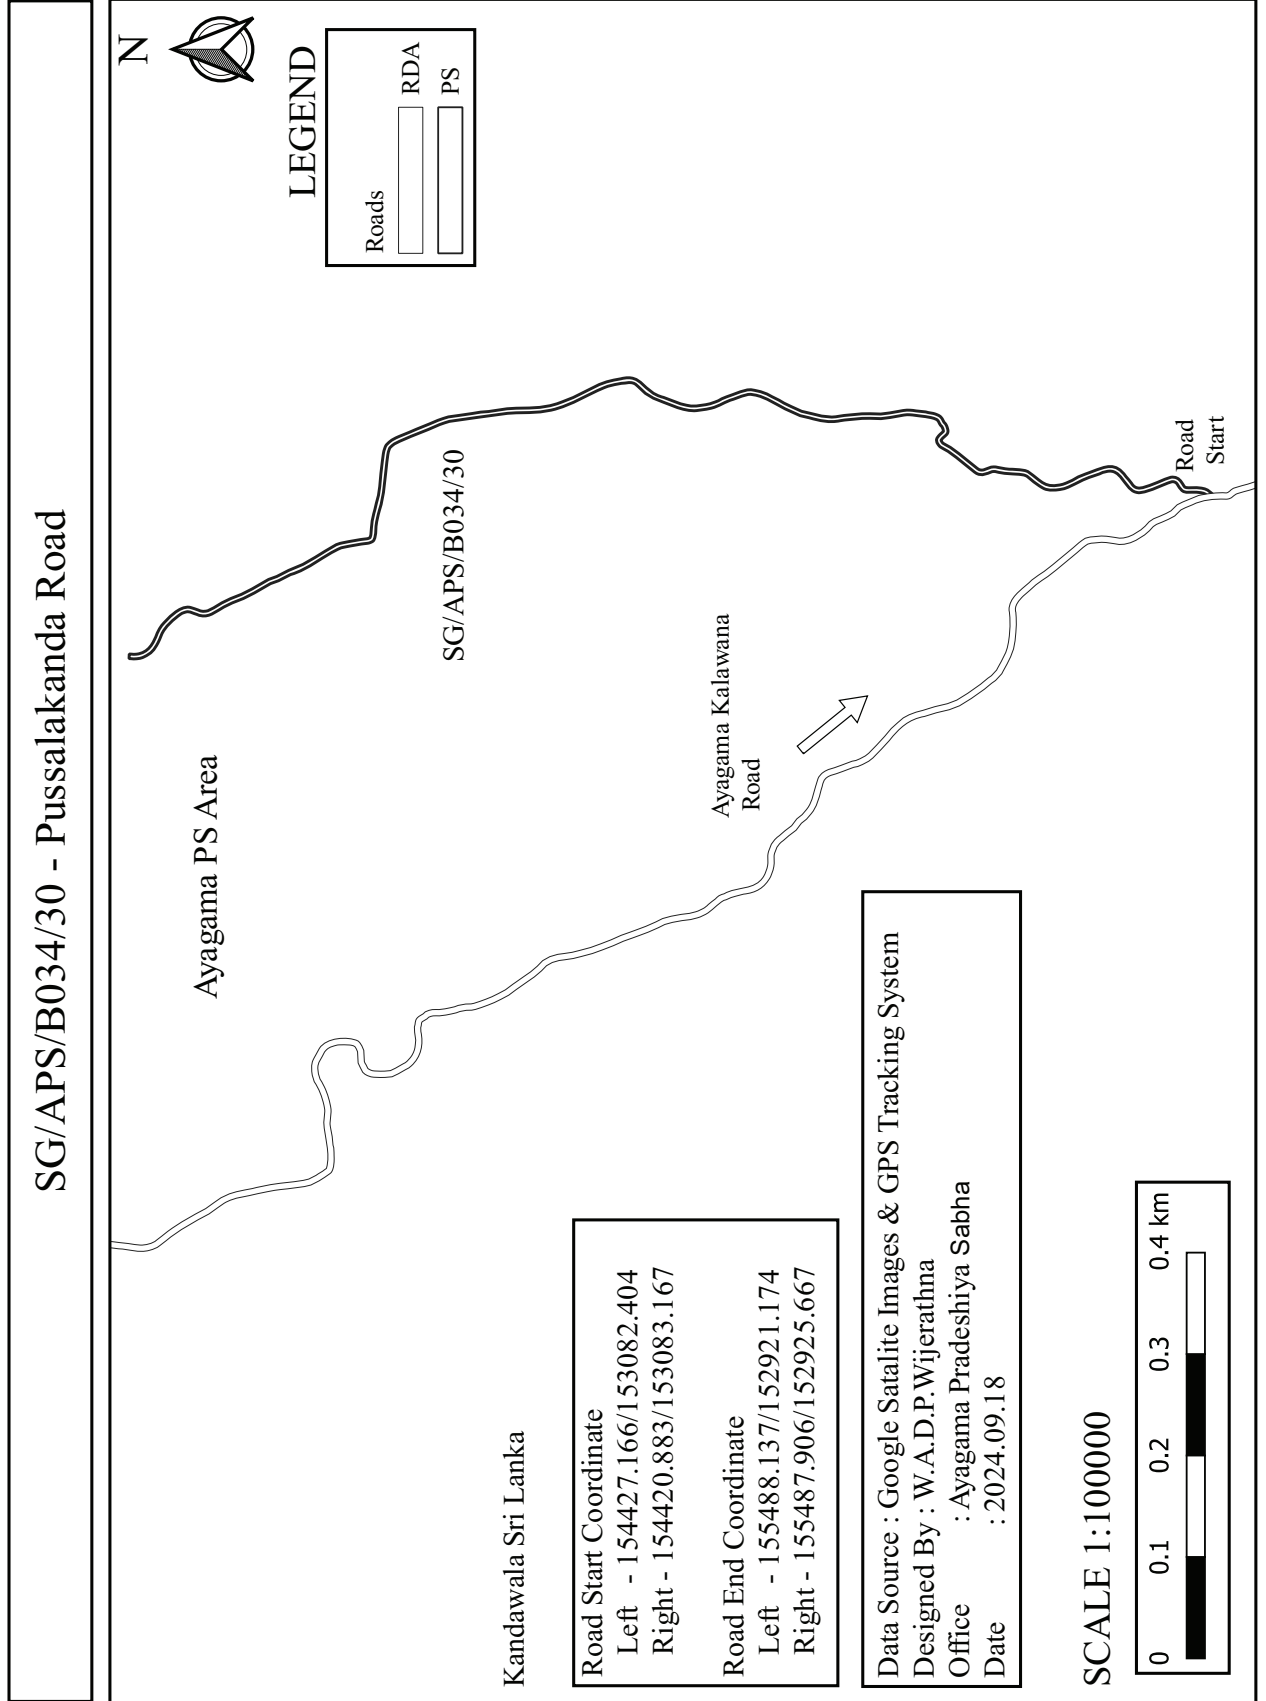


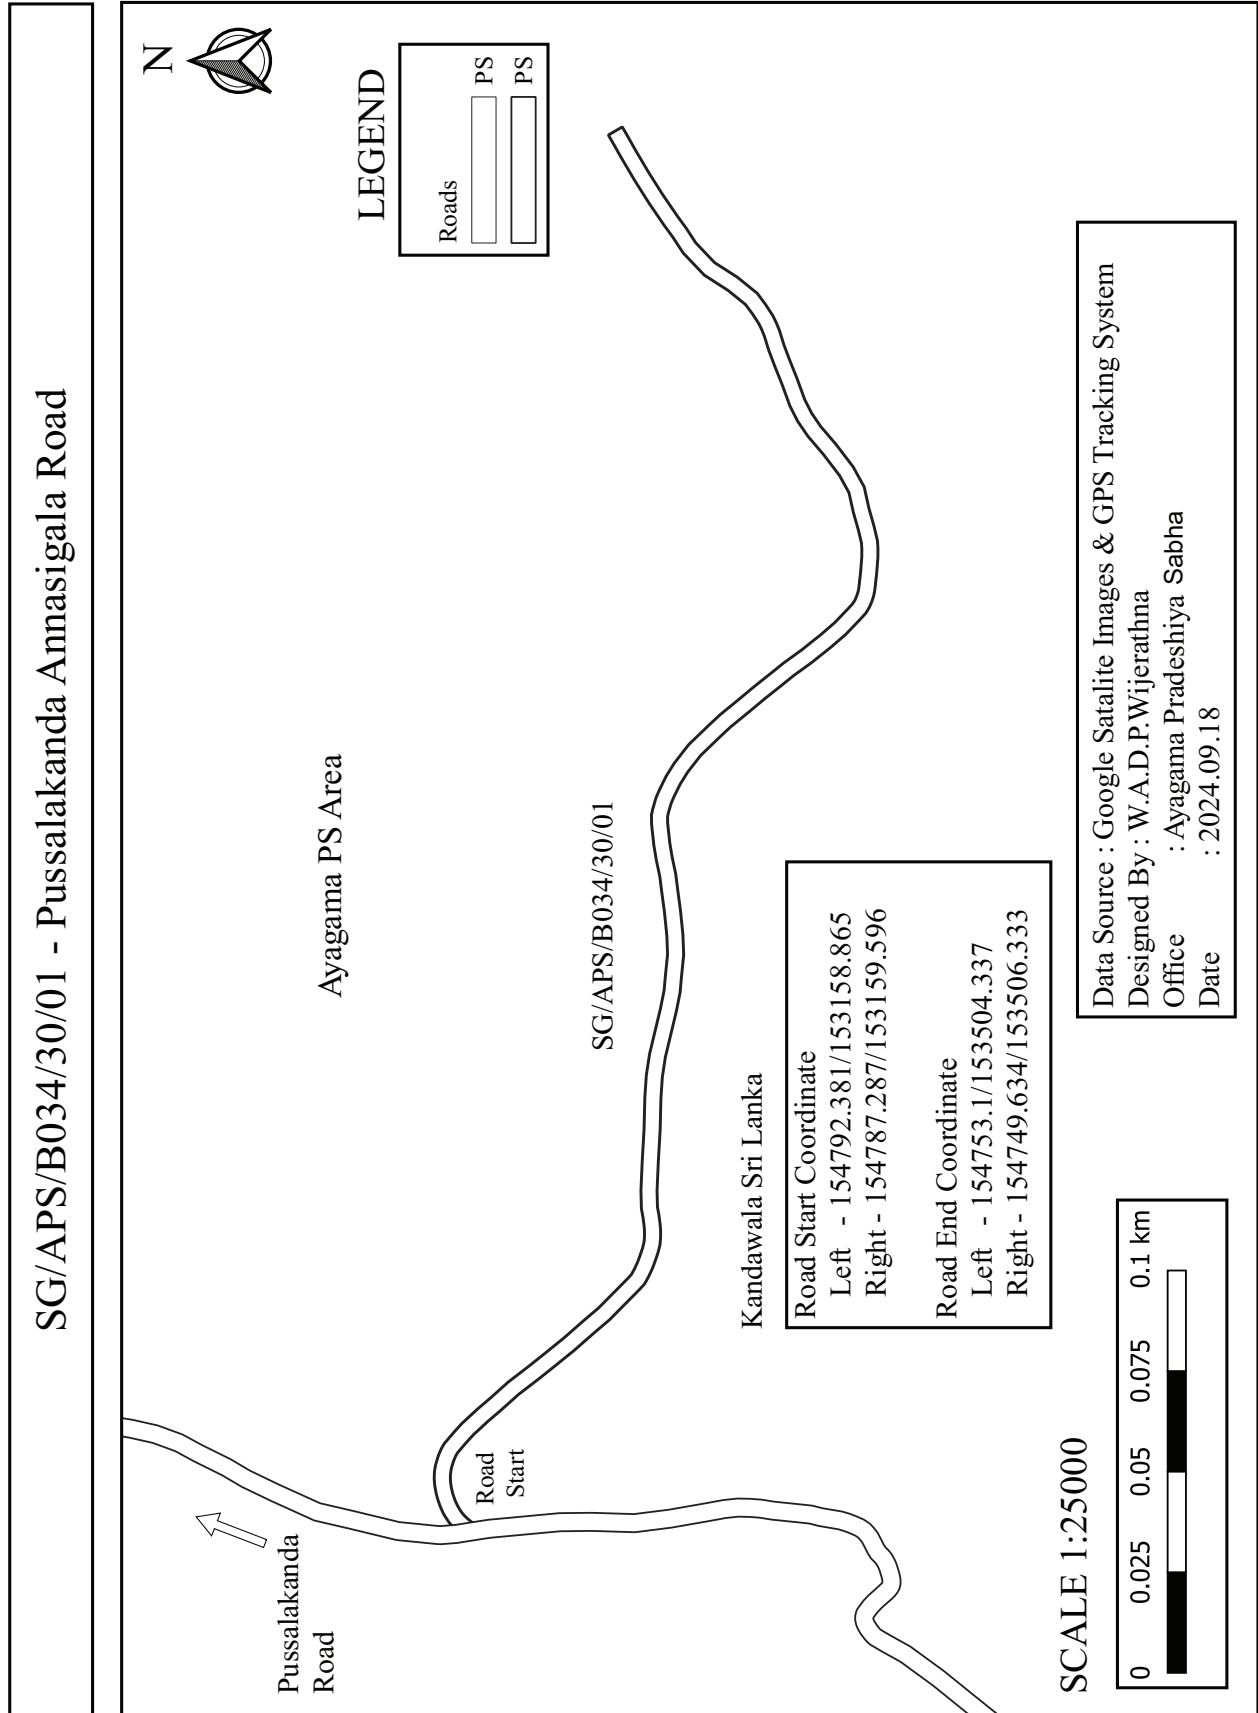


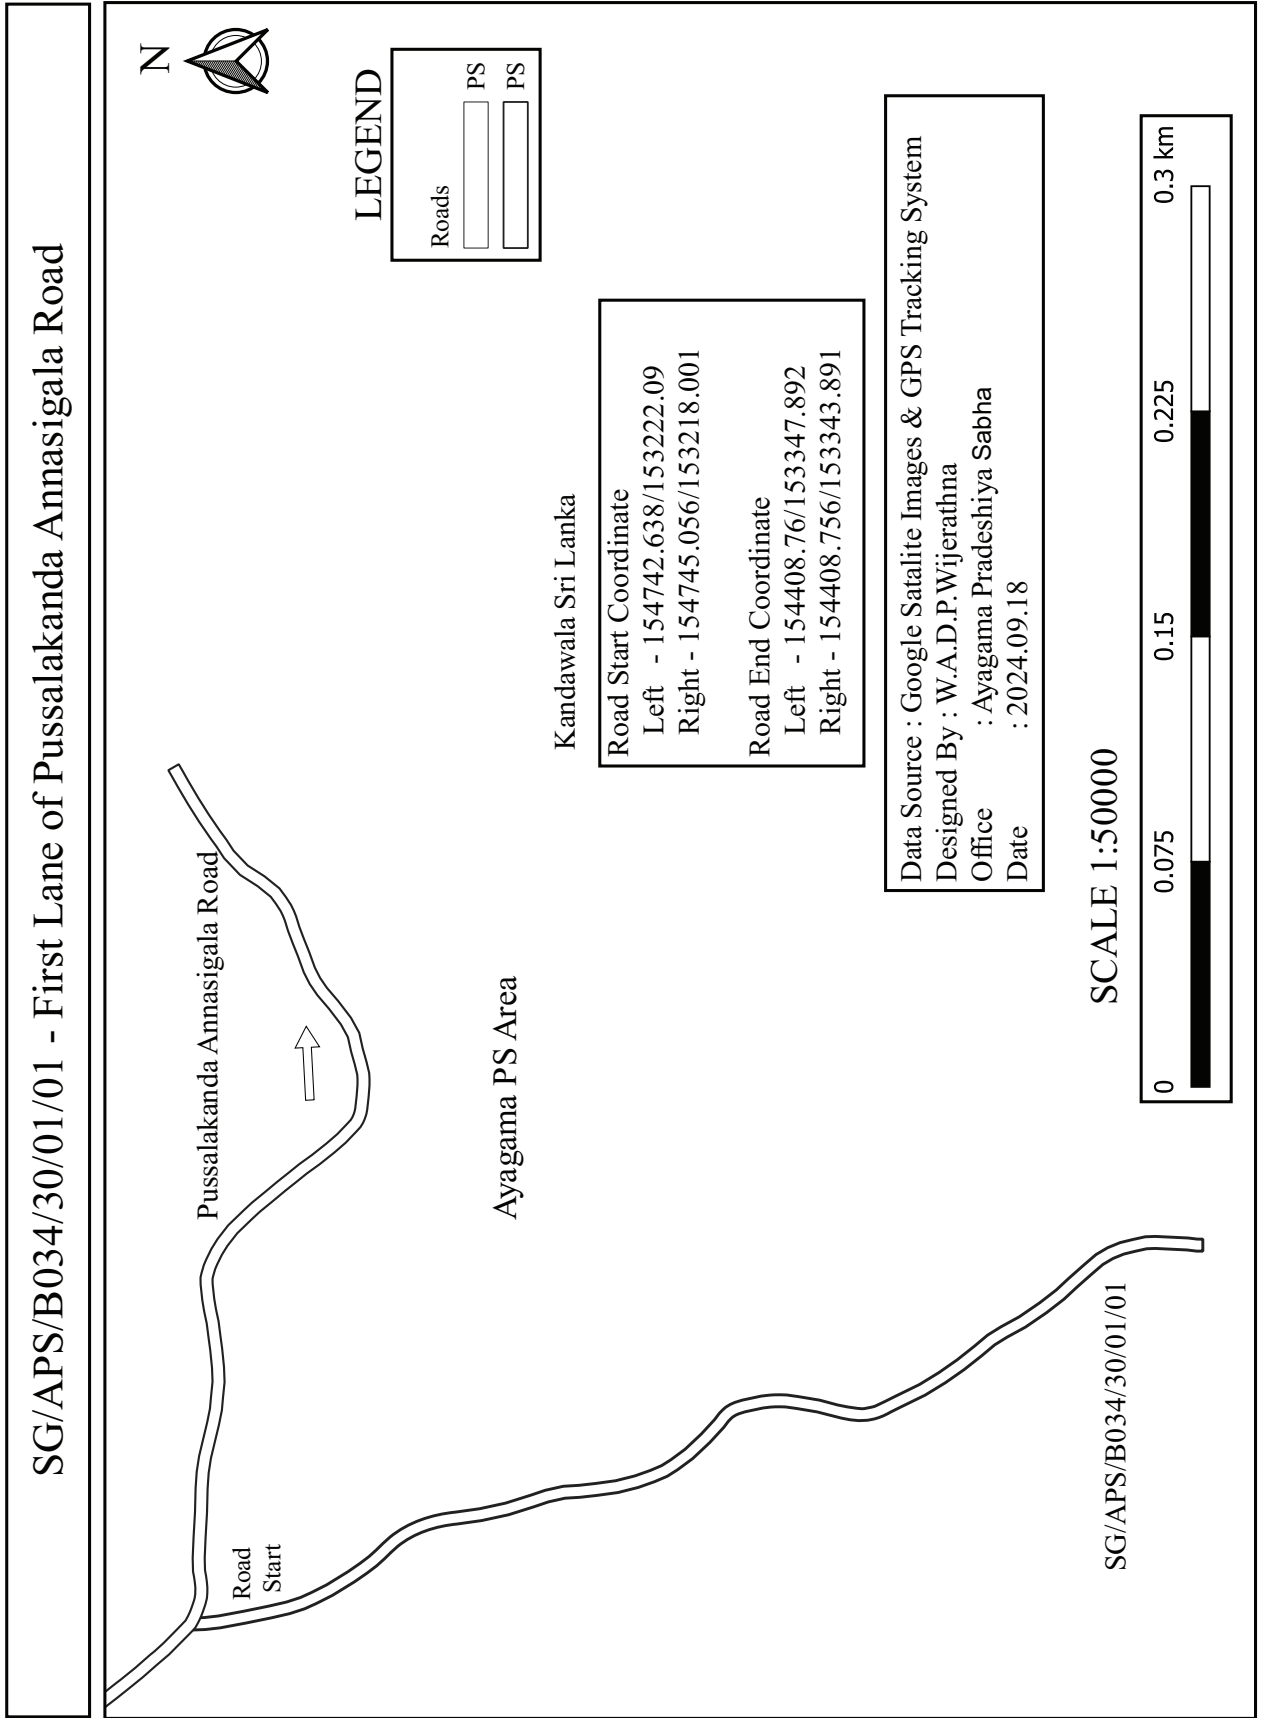

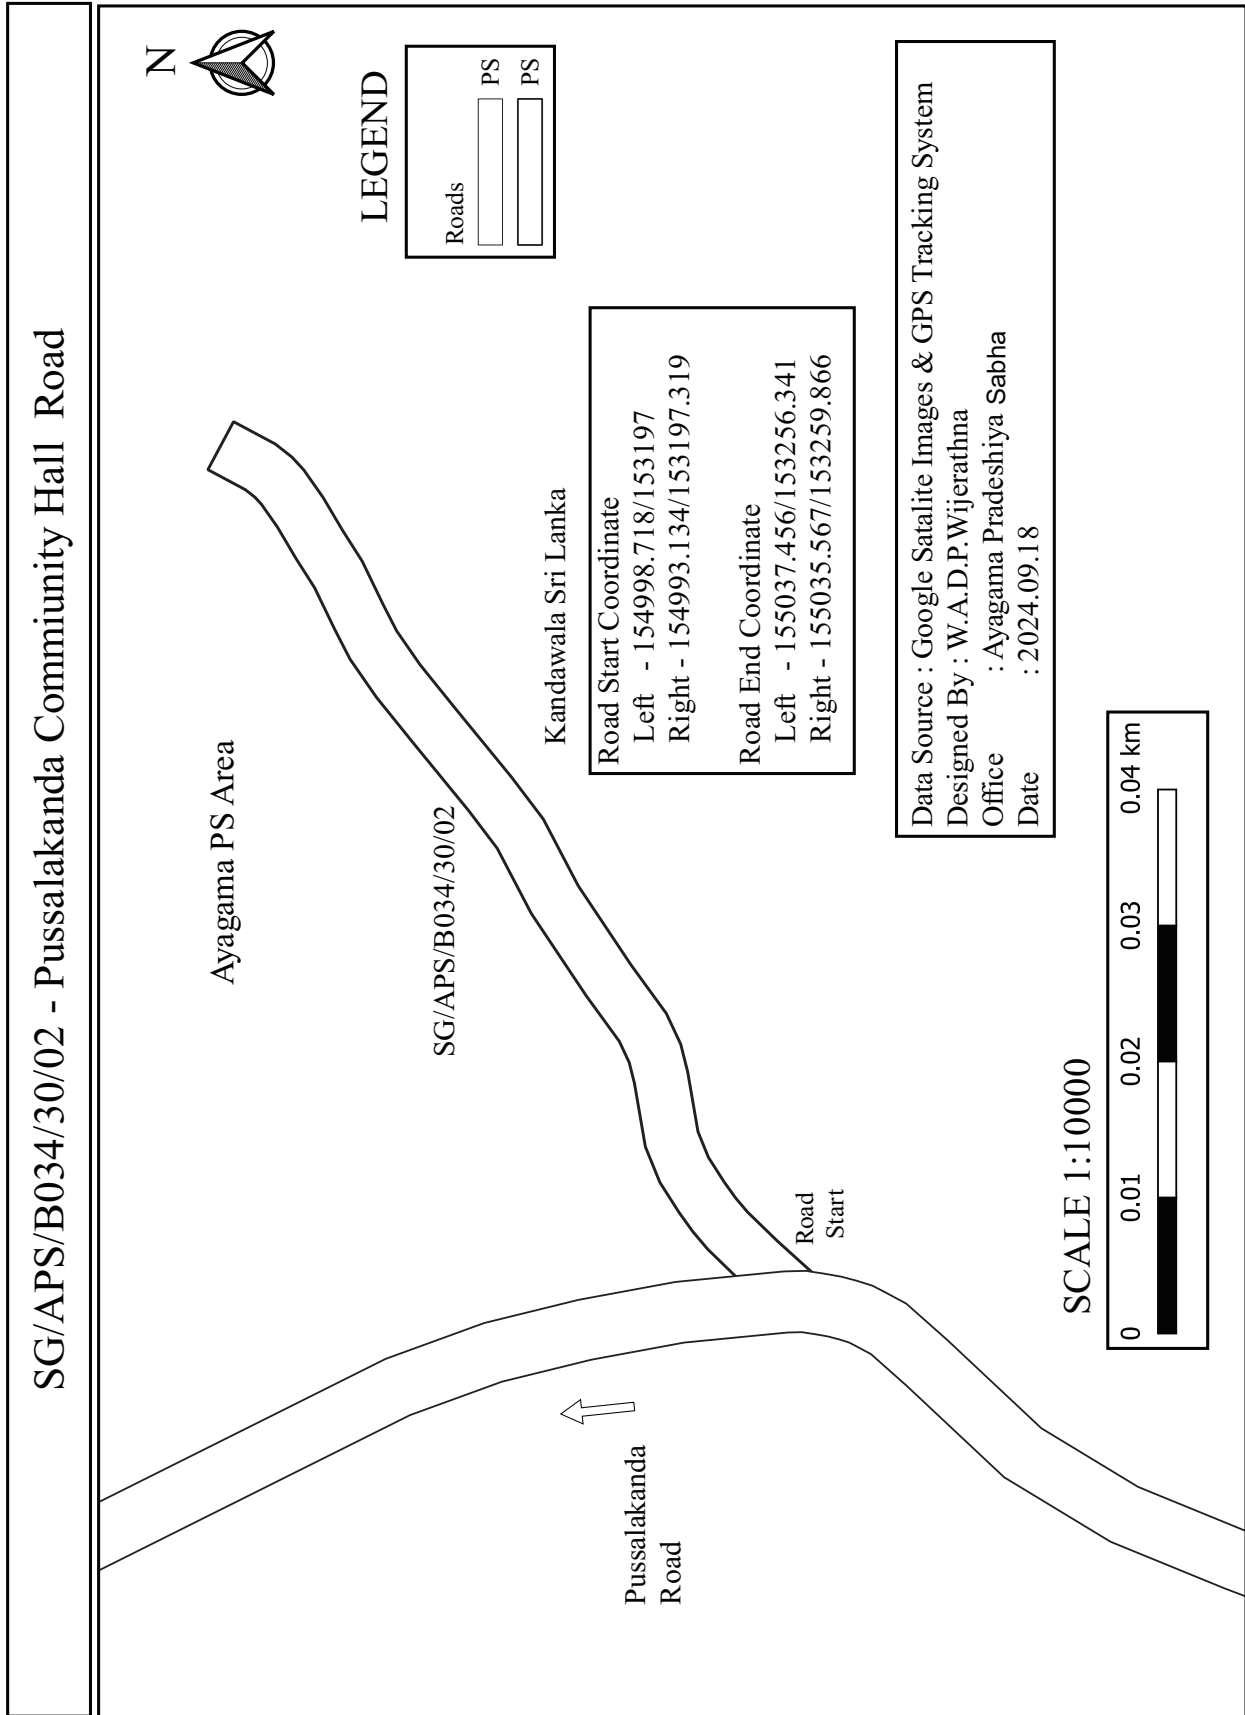


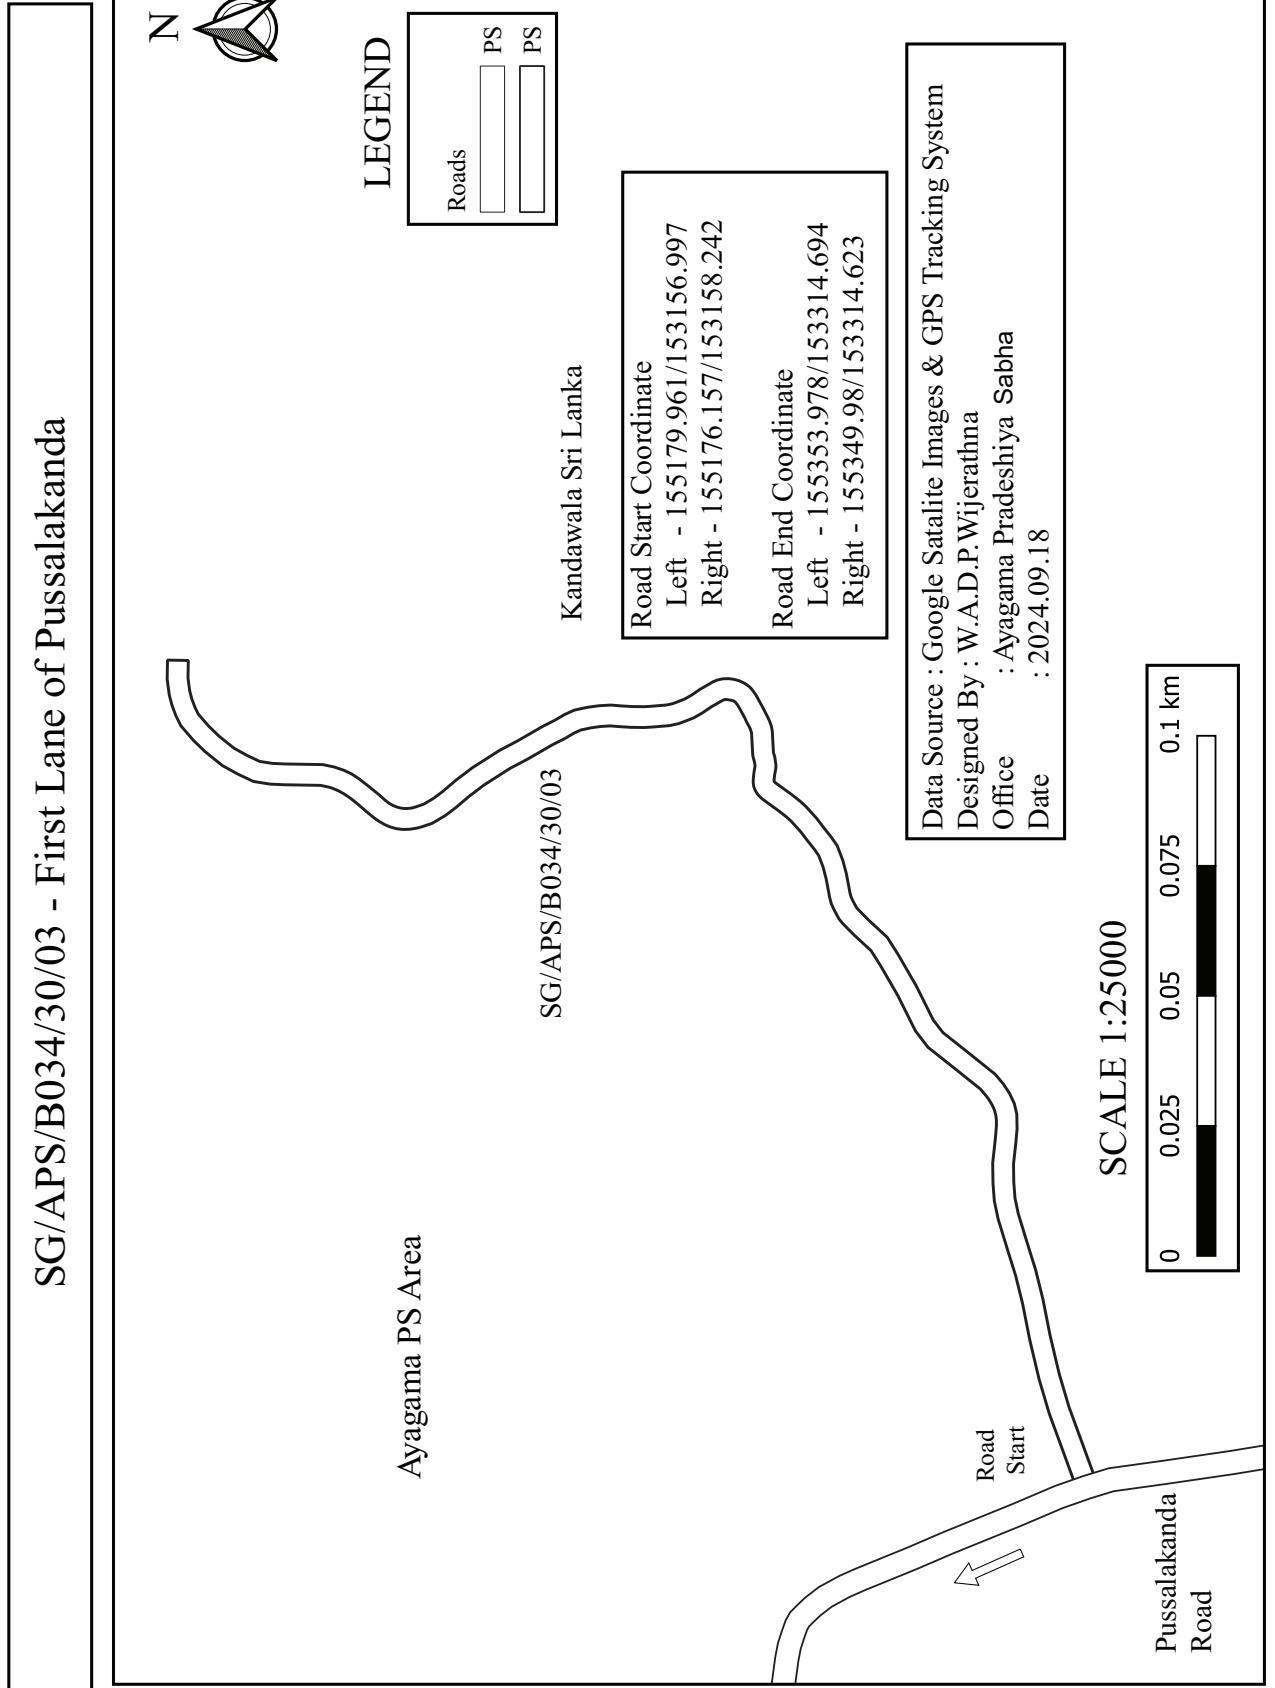

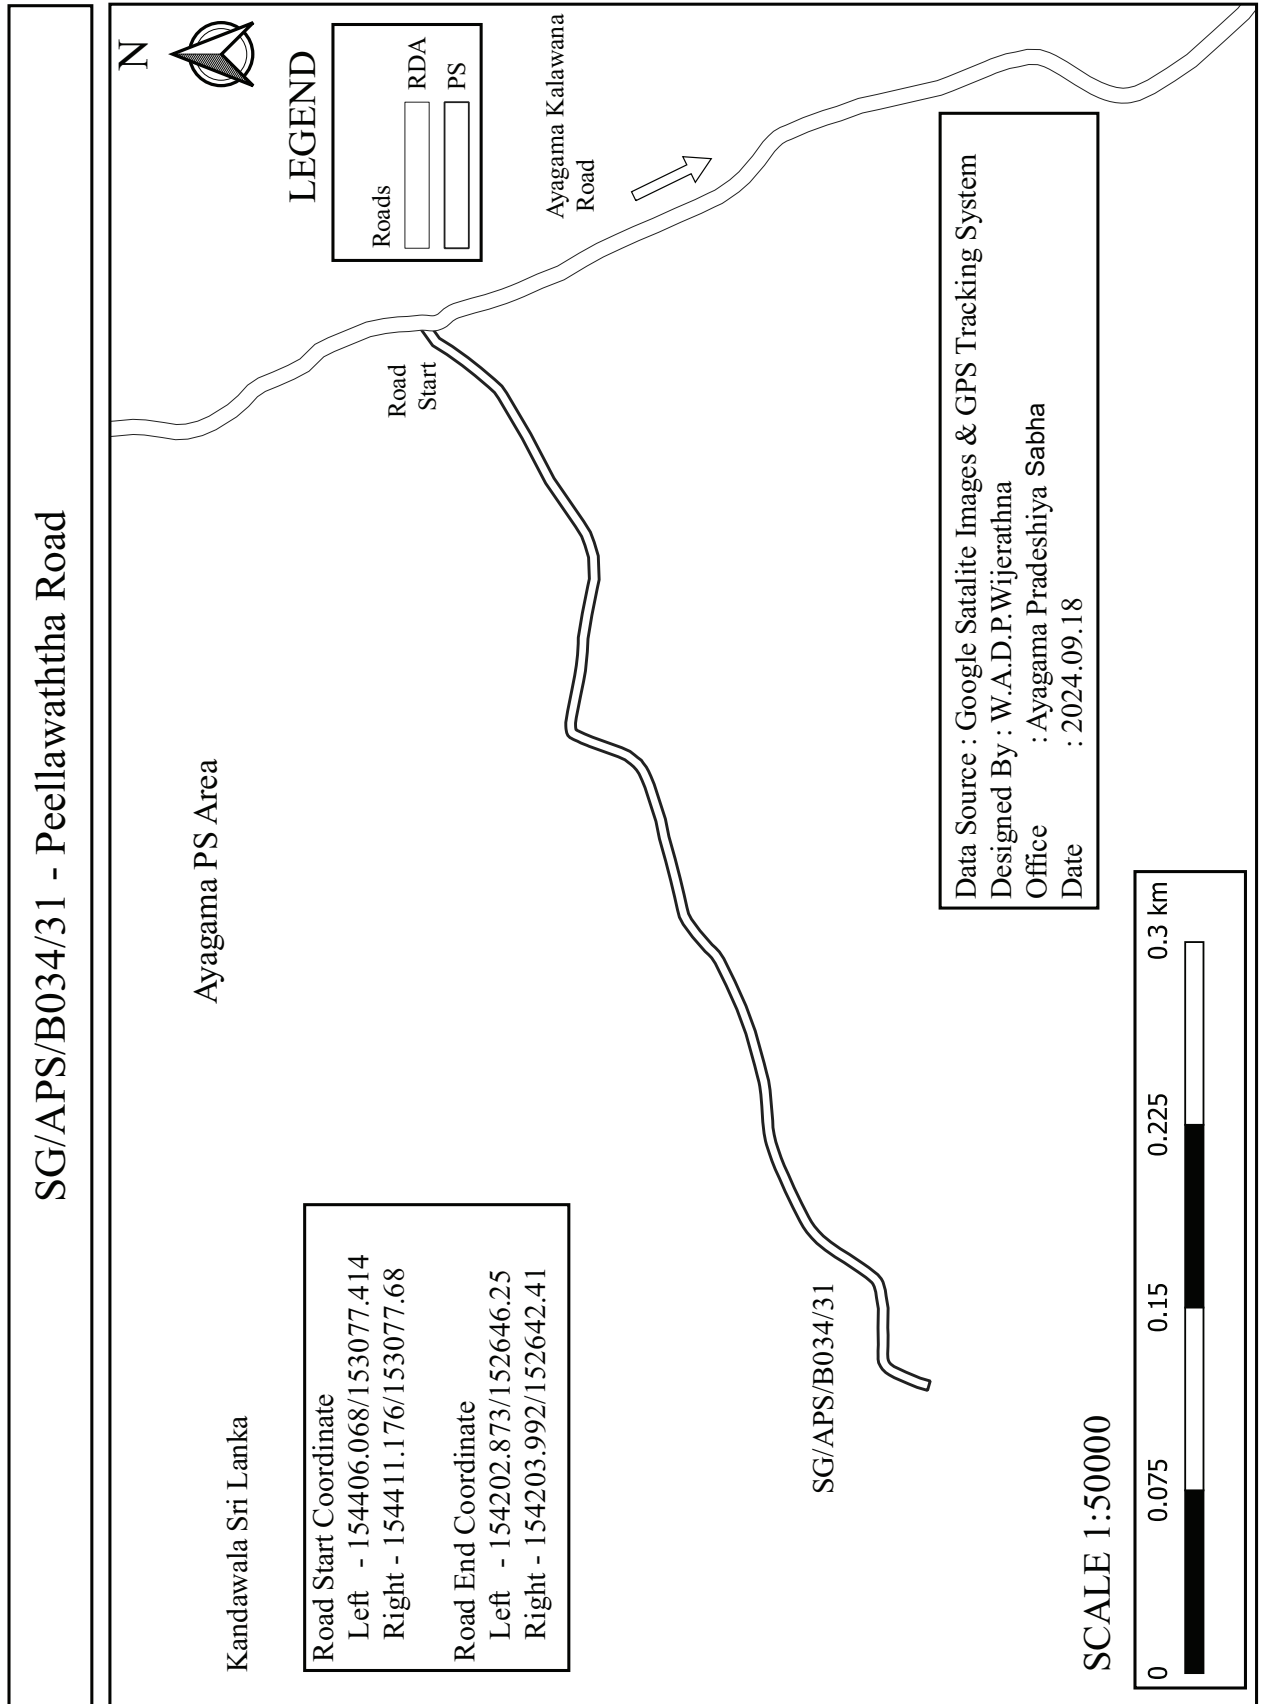

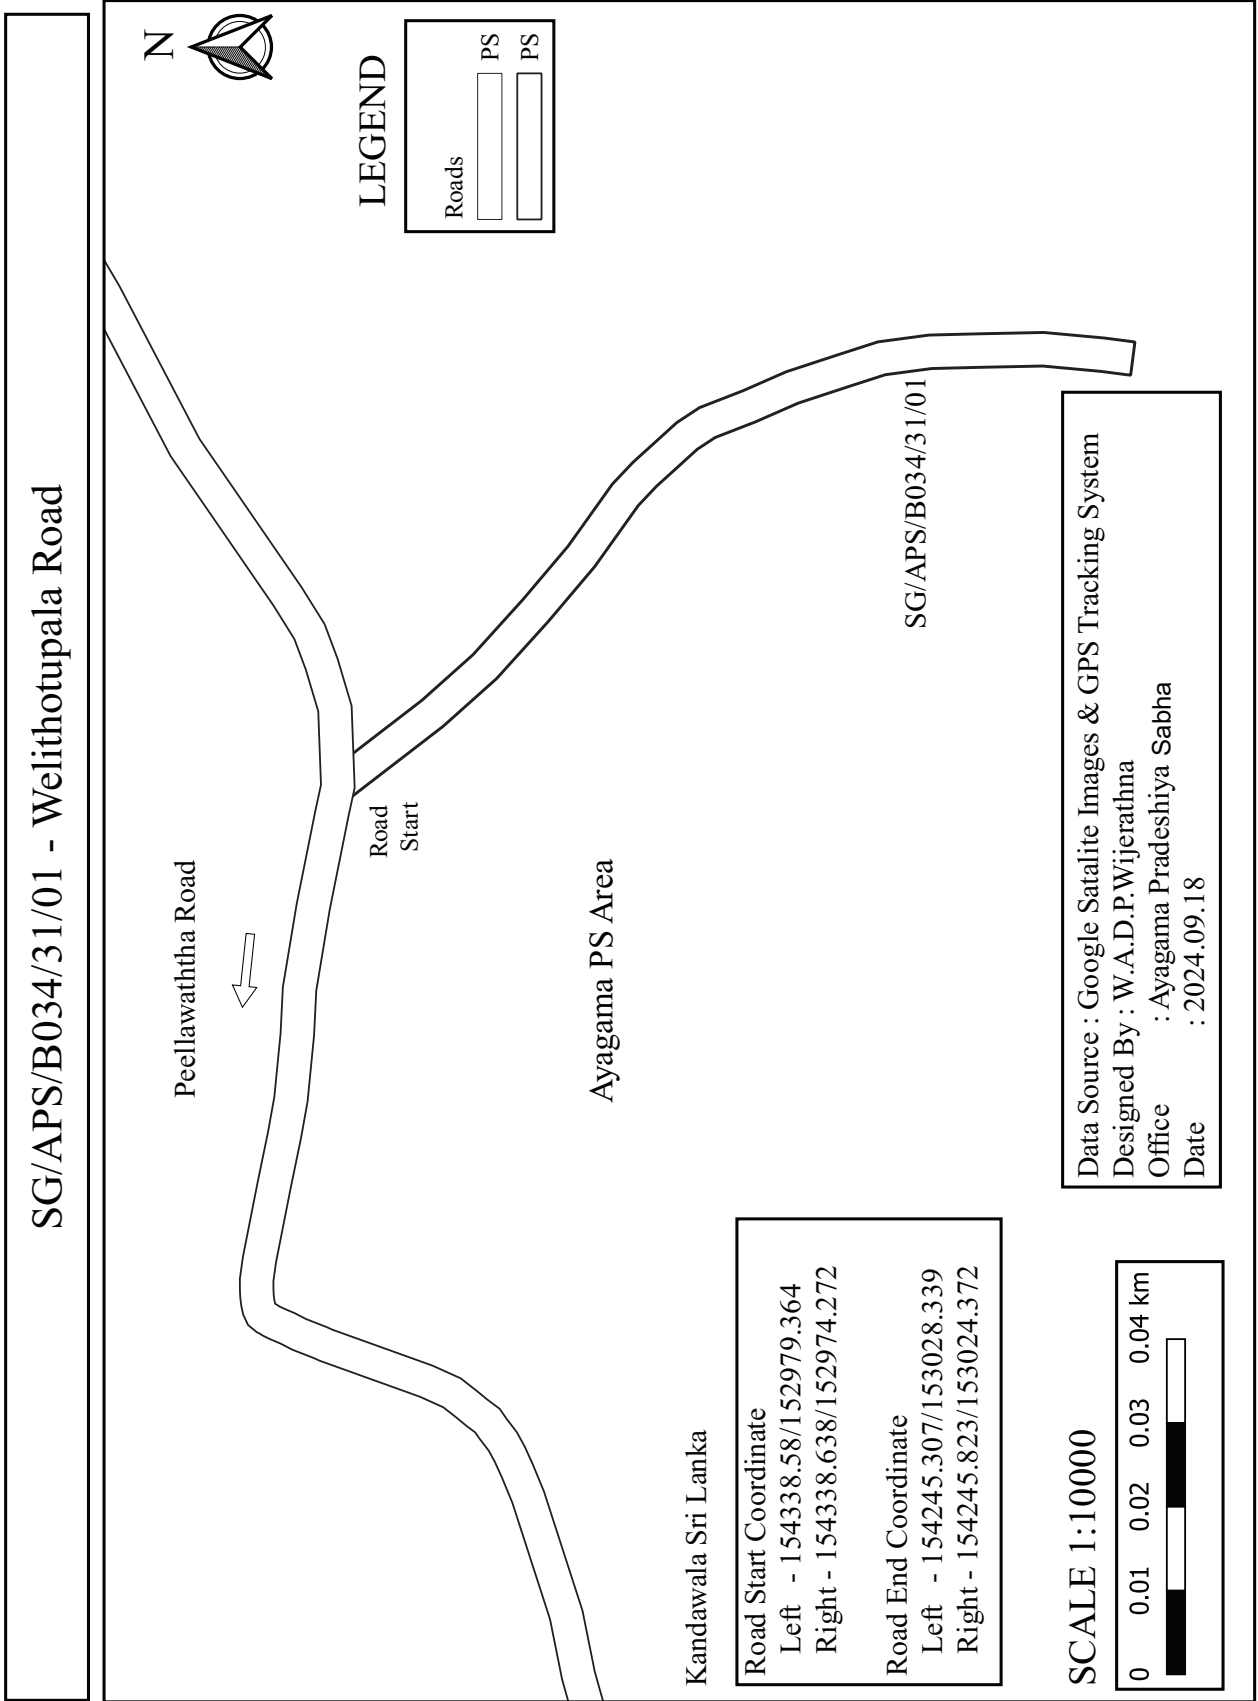

SG/APS/B034/31/02 - First Lane of Peellawaththa Road

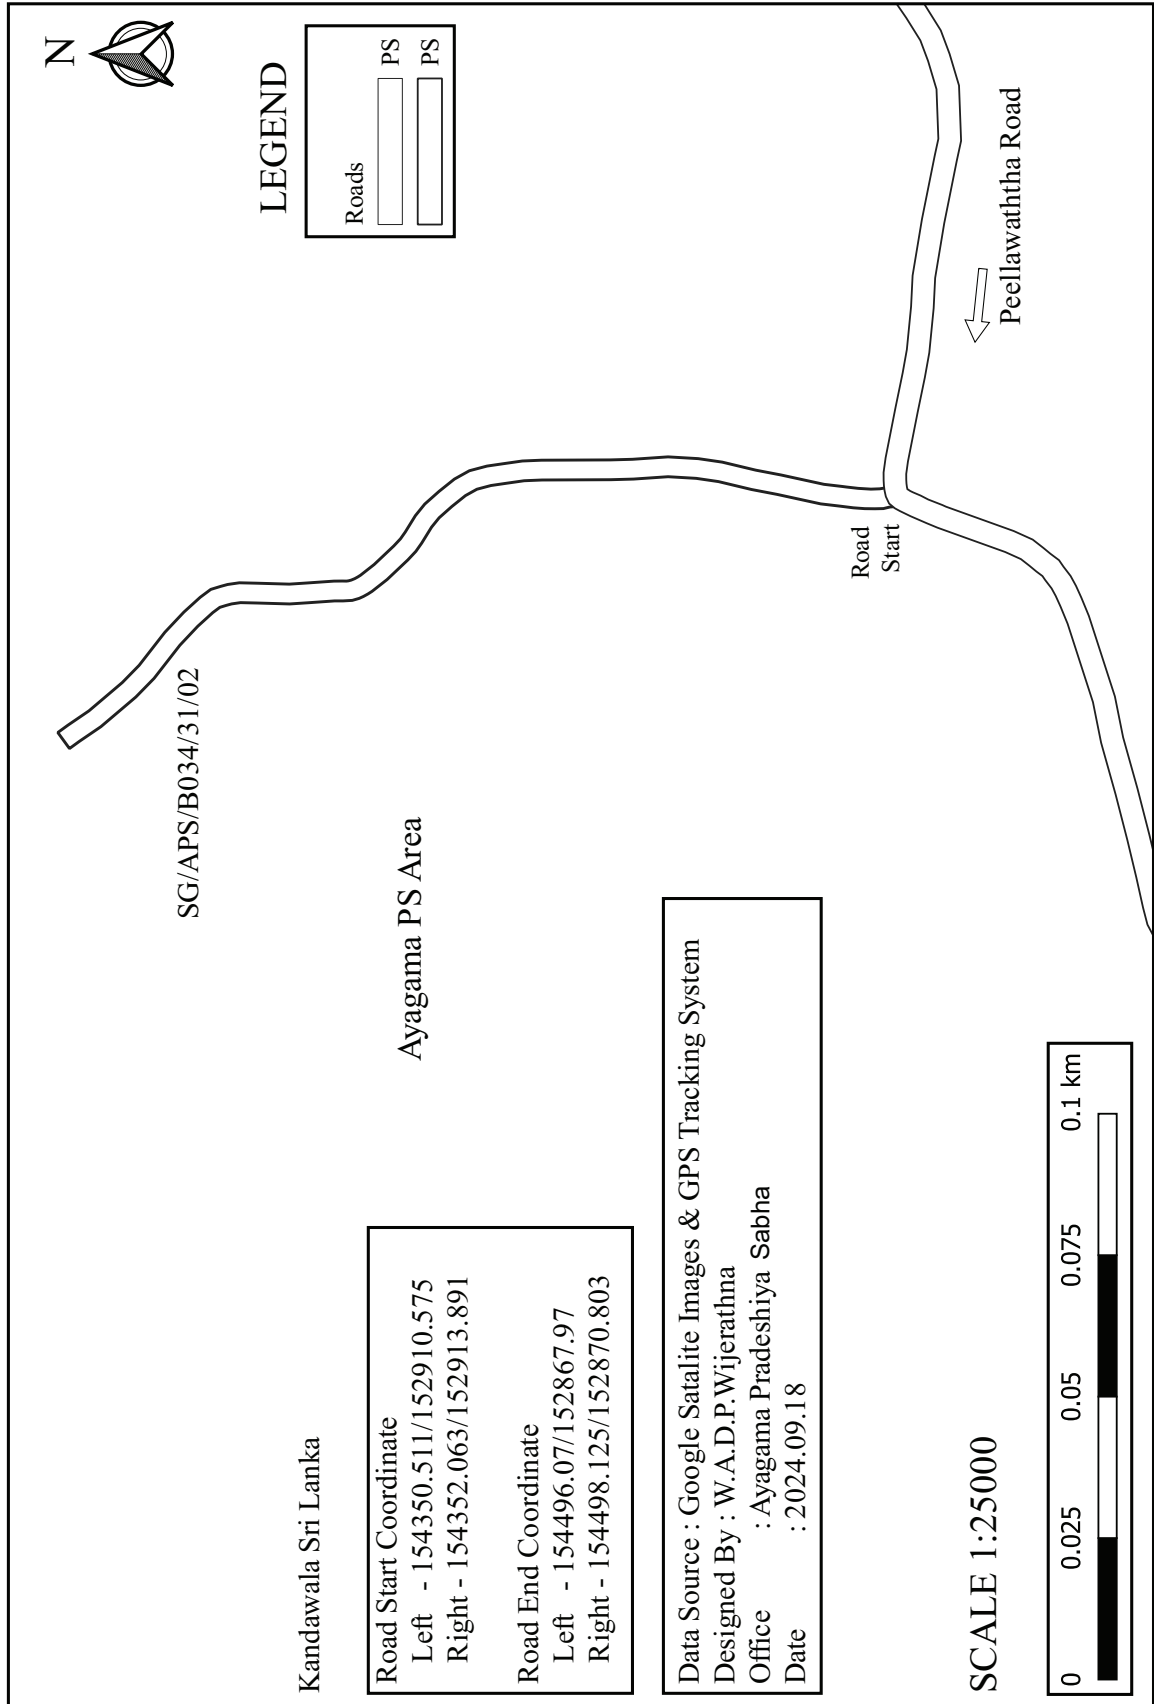

LEGEND

Roads

PS

1

Ayagama PS Area

SG/APS/B034/31/03

Road / Start

Peellawaththa Road

SG/APS/B034/31/03 - Lindapitiya Road

Kandawala Sri Lanka

Road Start Coordinate

Left - 154304.71/152834.973

Right - 154305.897/152837.782

Road End Coordinate

Left - 154522.292/152705.741

Right - 154521.95/152708.722

Data Source : Google Satalite Images & GPS Tracking System

Designed By : W.A.D.P.Wijerathna

Office : Ayagama Pradeshiya Sabha


Date: 2024.09.18


SCALE 1:25000


0	0.025	0.05	0.075	0.1 km
---	-------	------	-------	--------





SG/APS/B034/31/03/01 - Lindapitiya Aranya Road

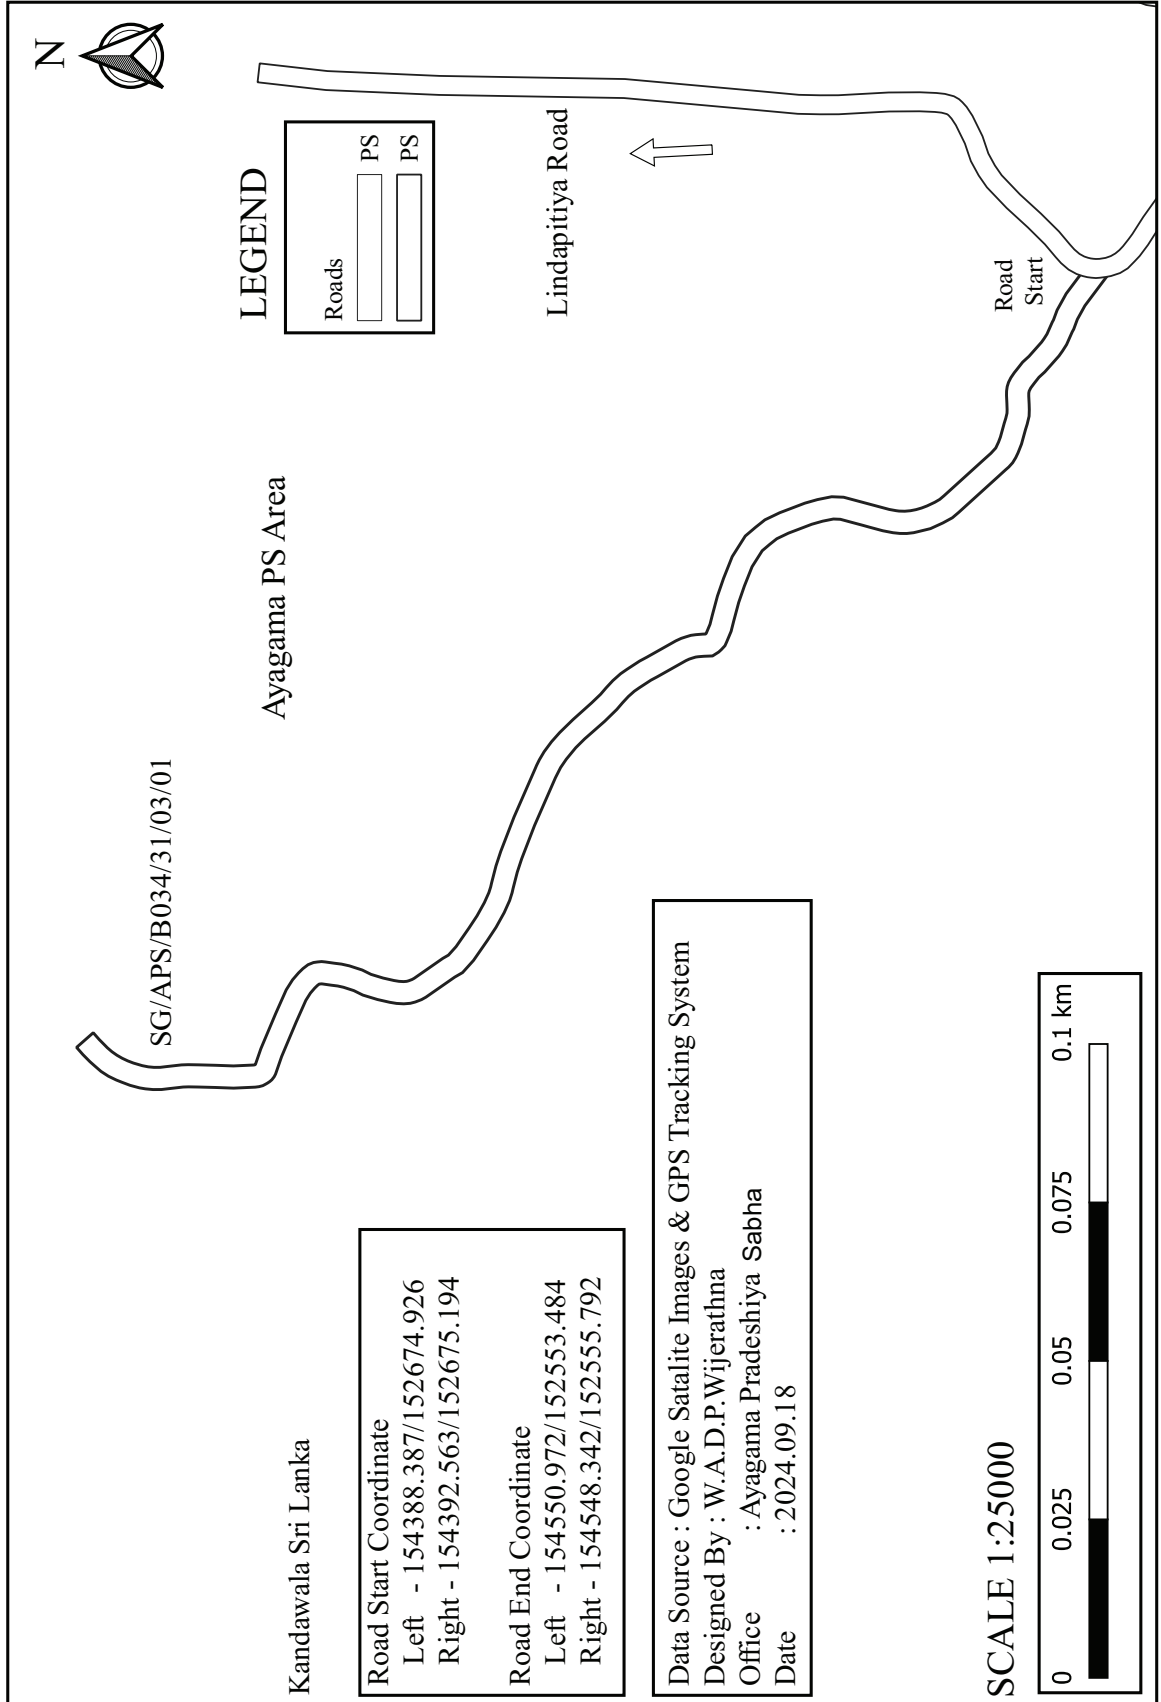


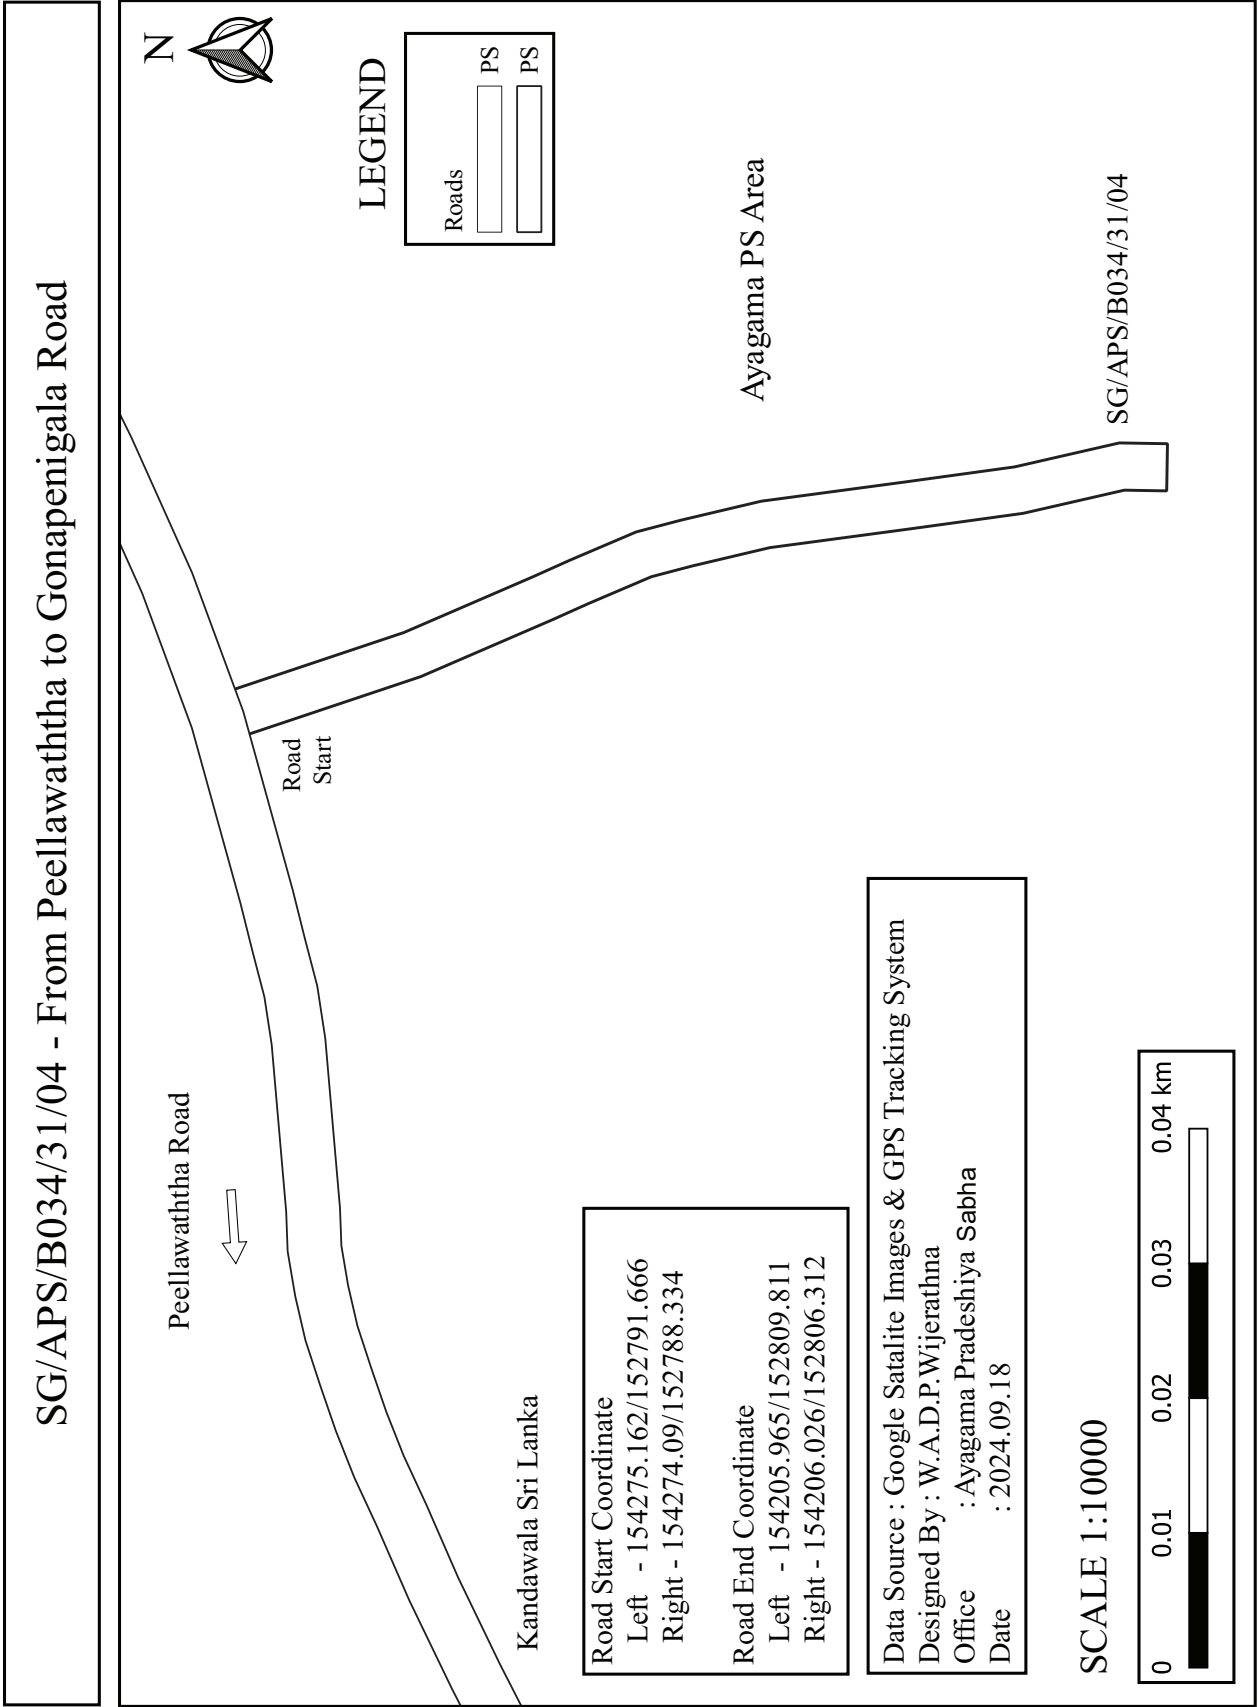

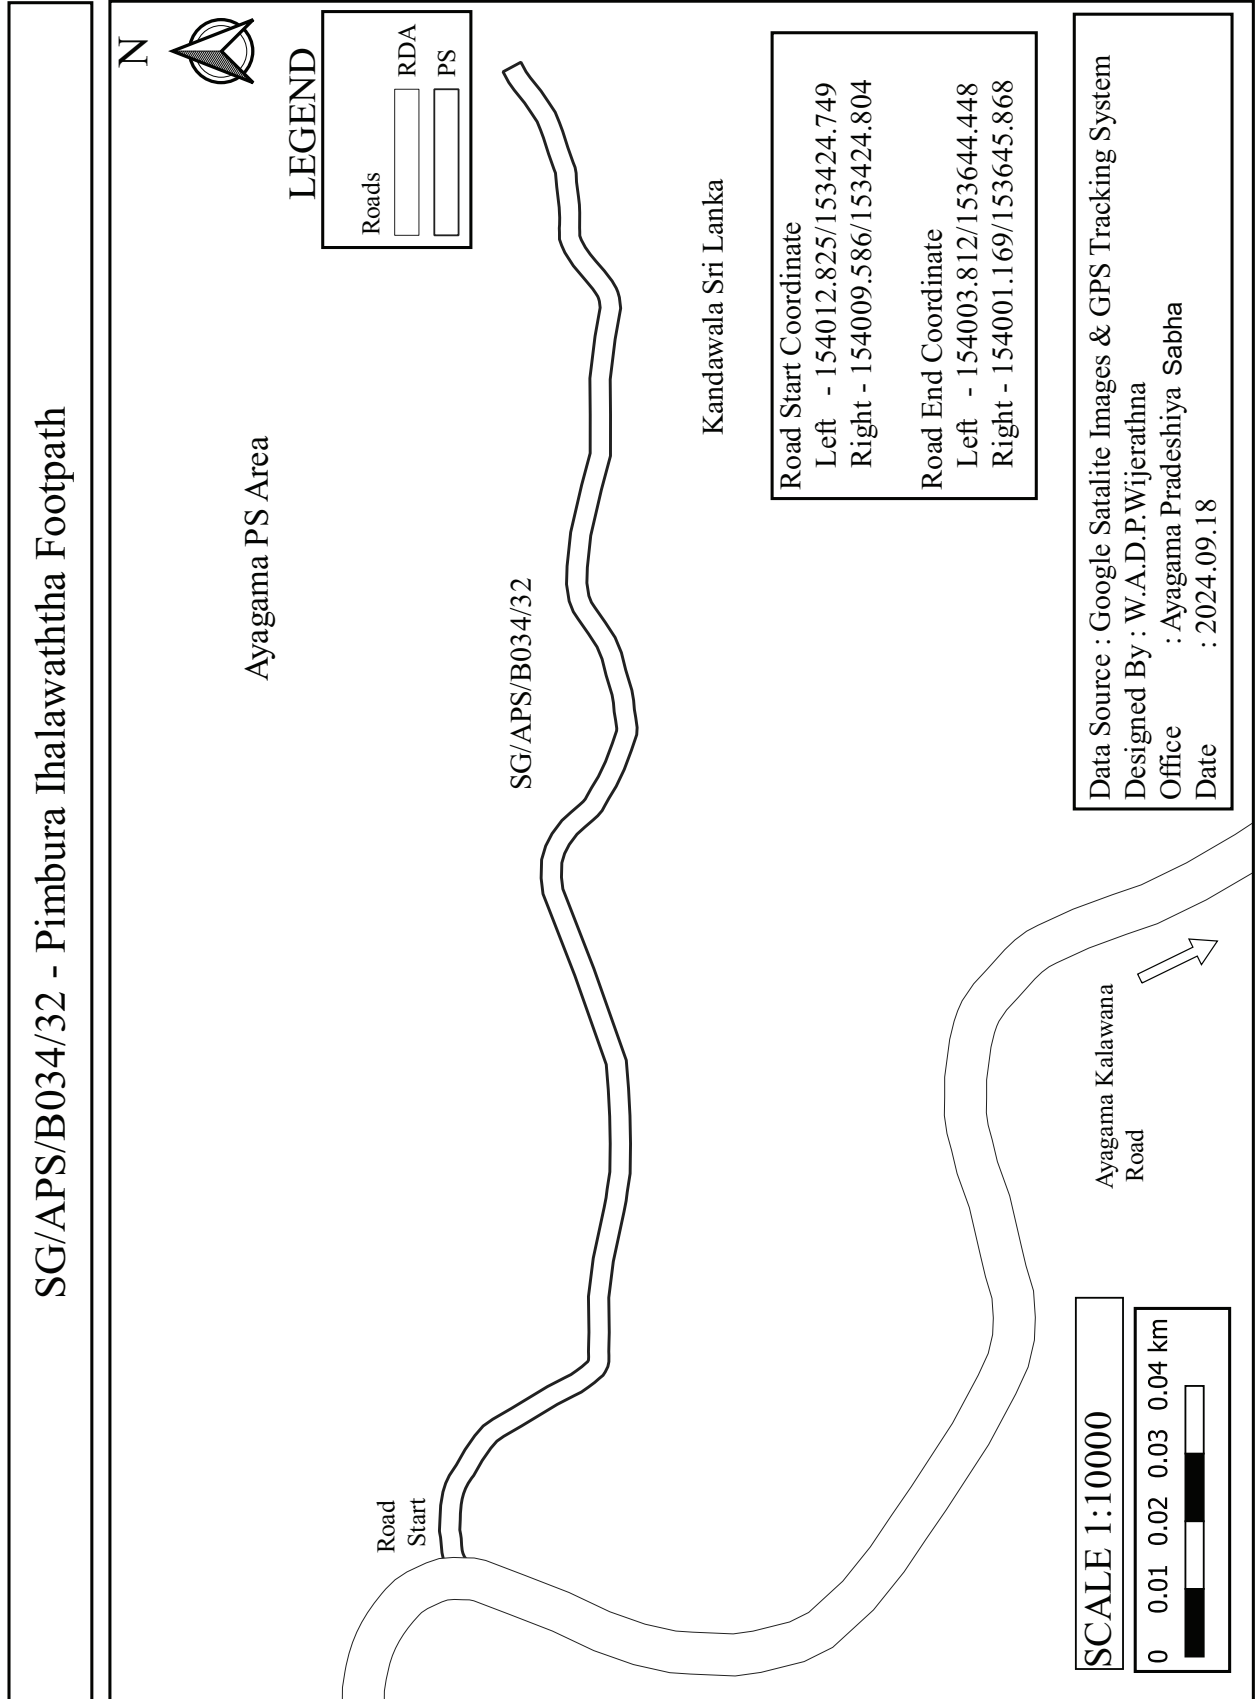


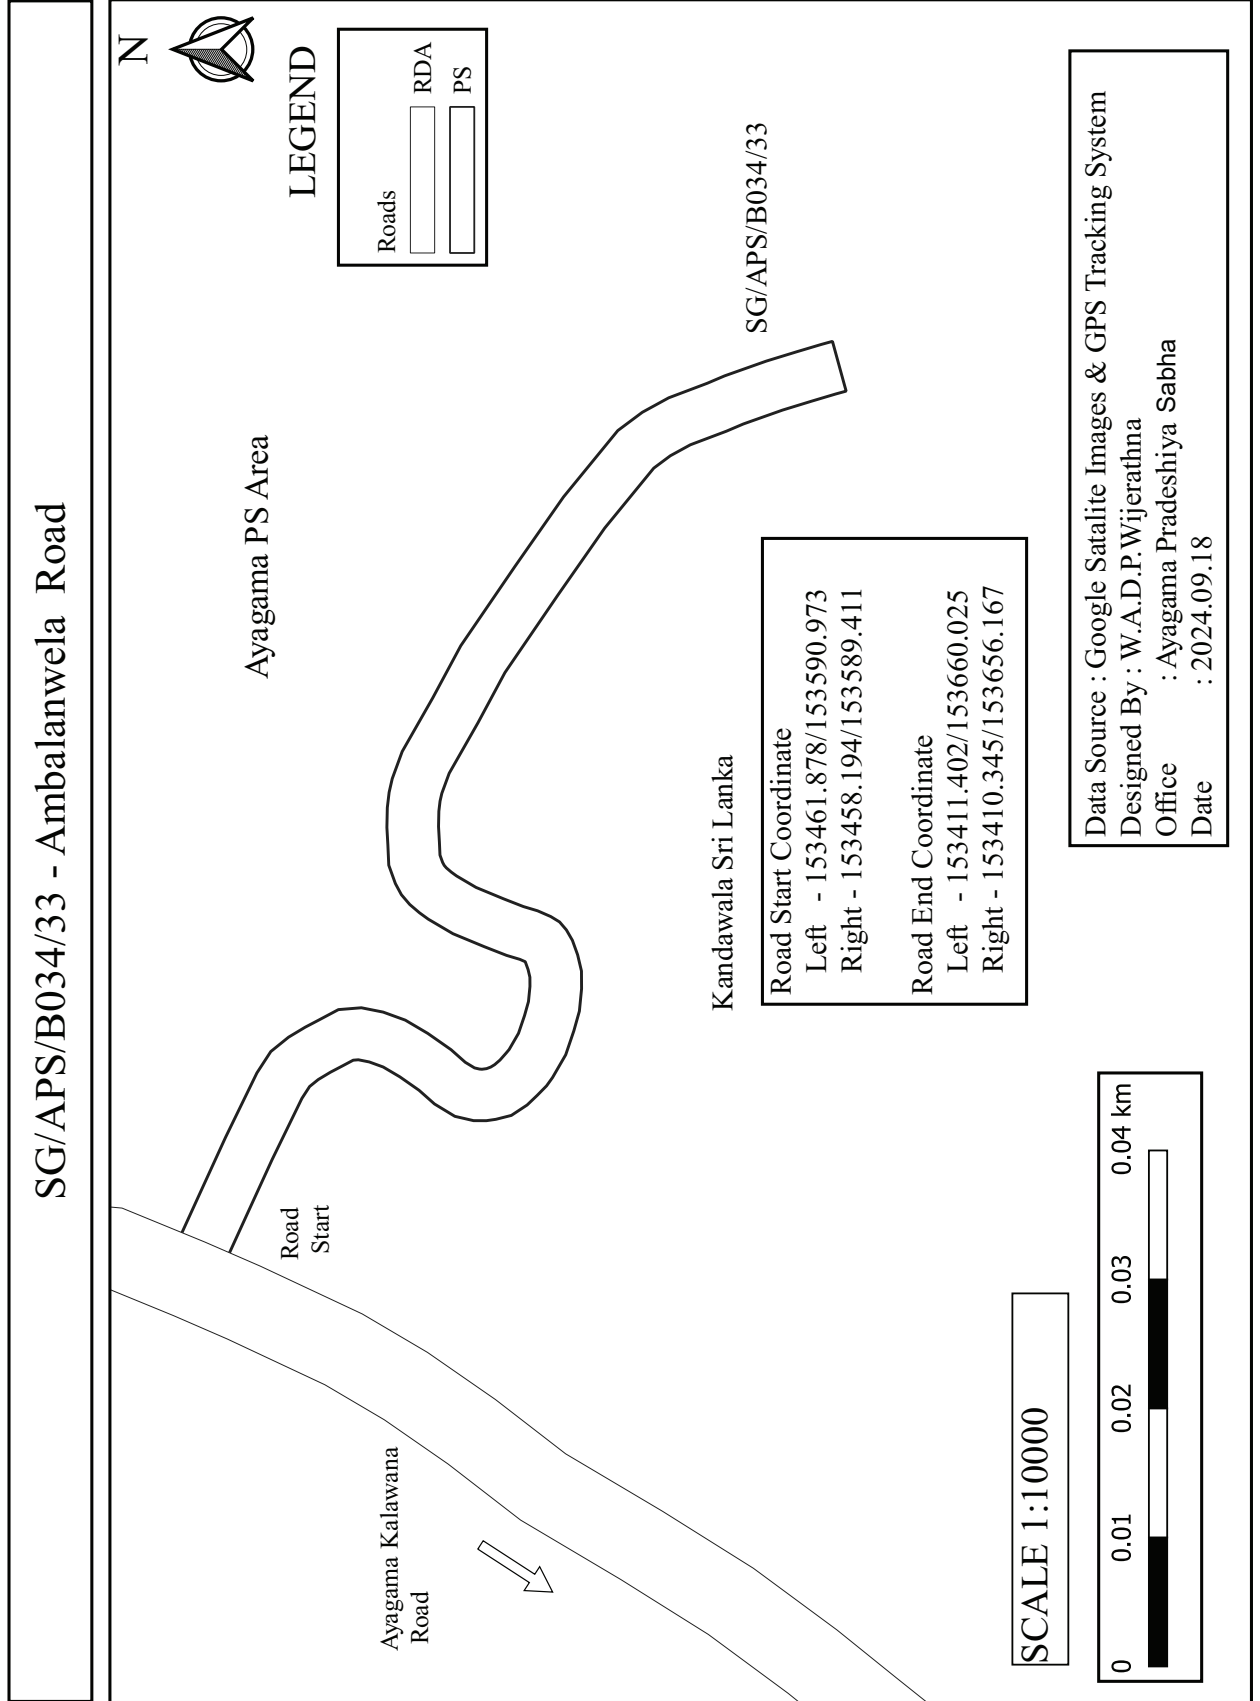


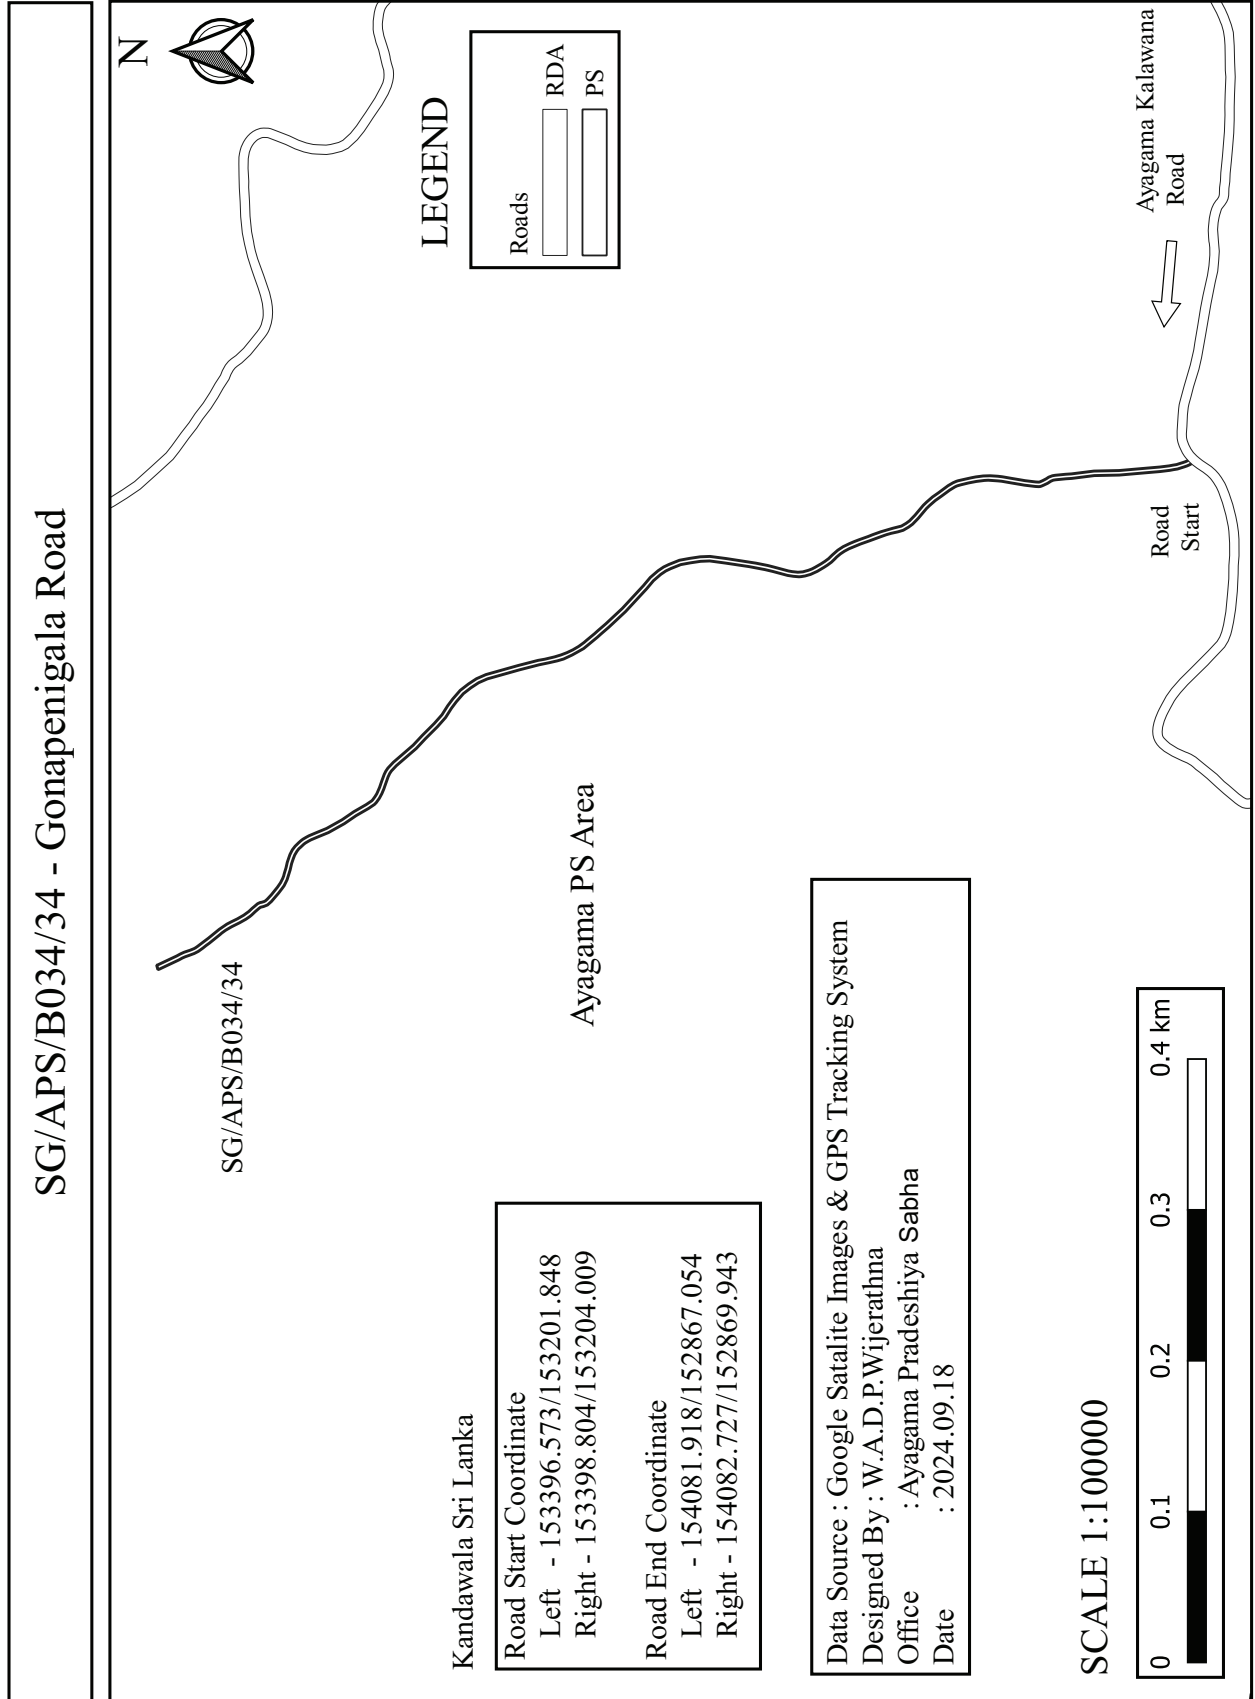


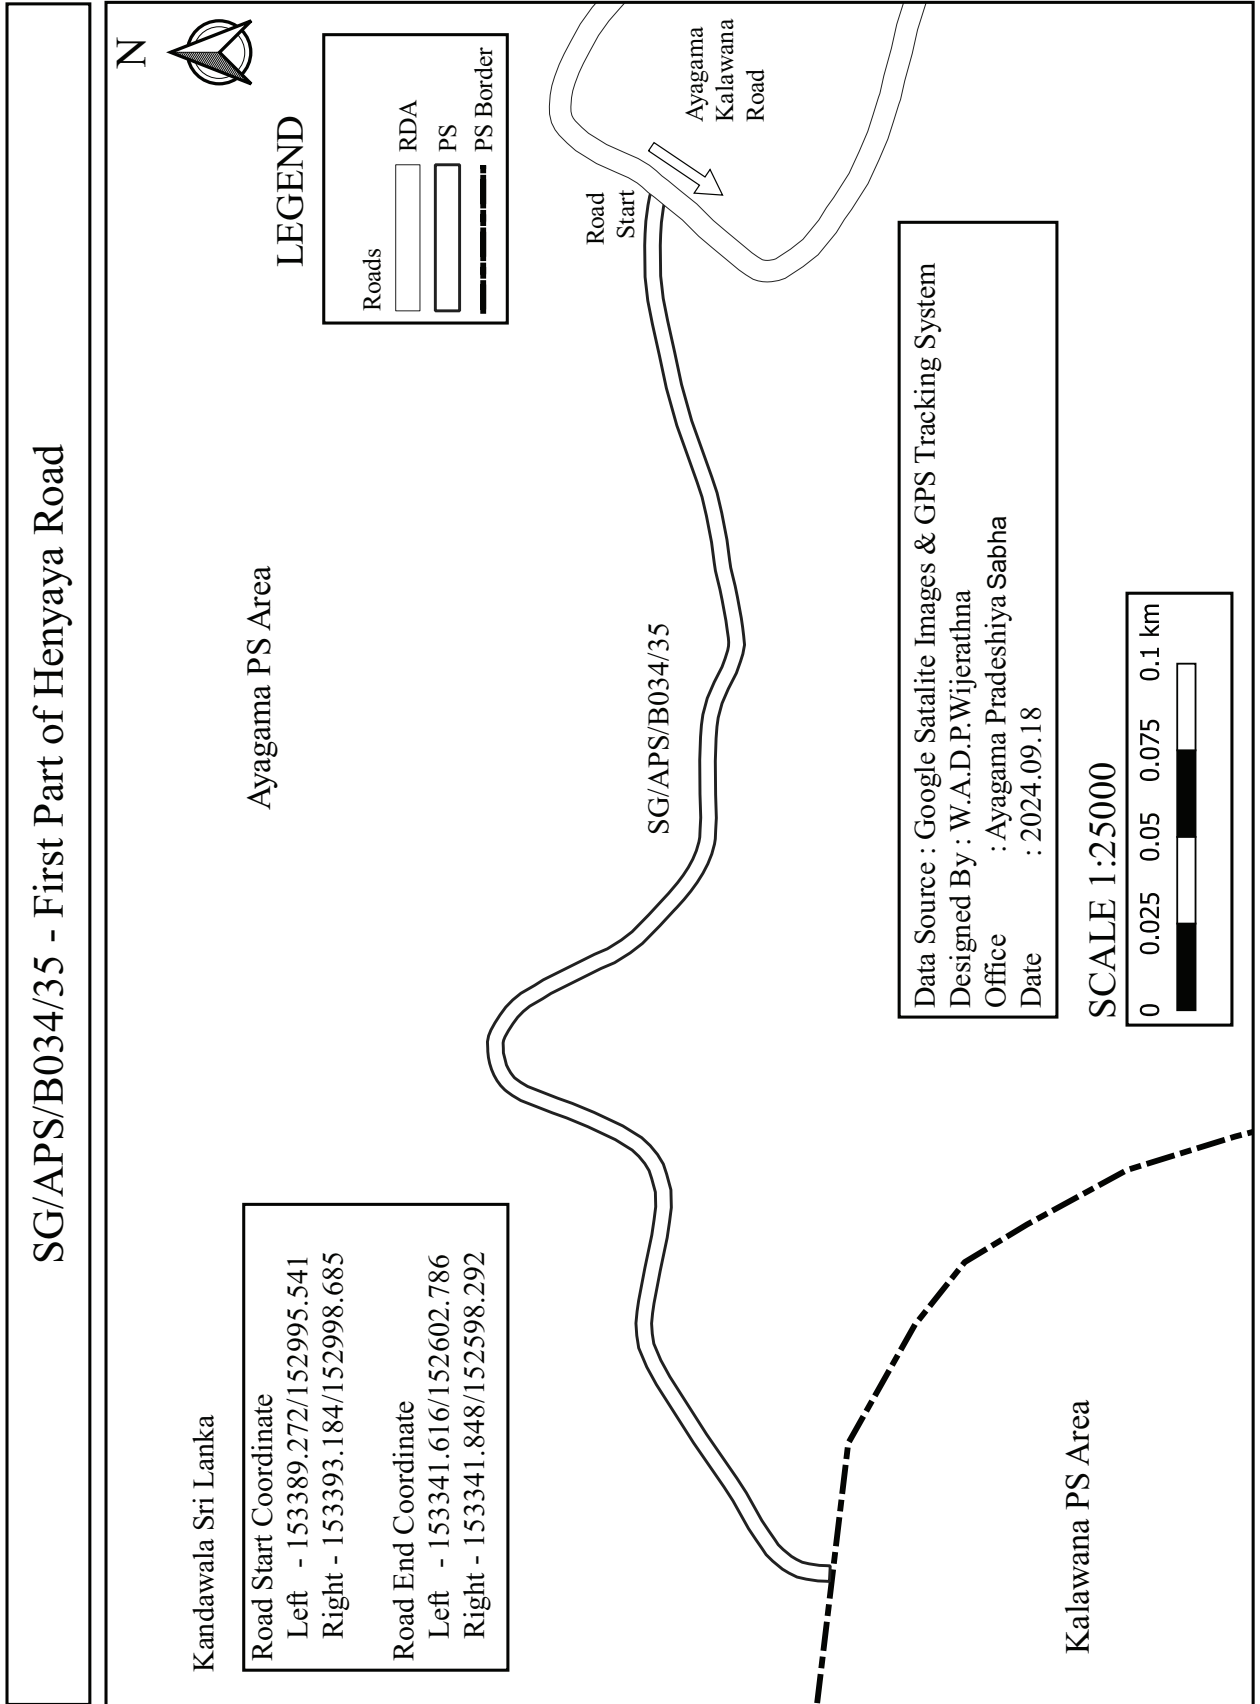


SG/APS/B034/35/01 - Manakanda Road

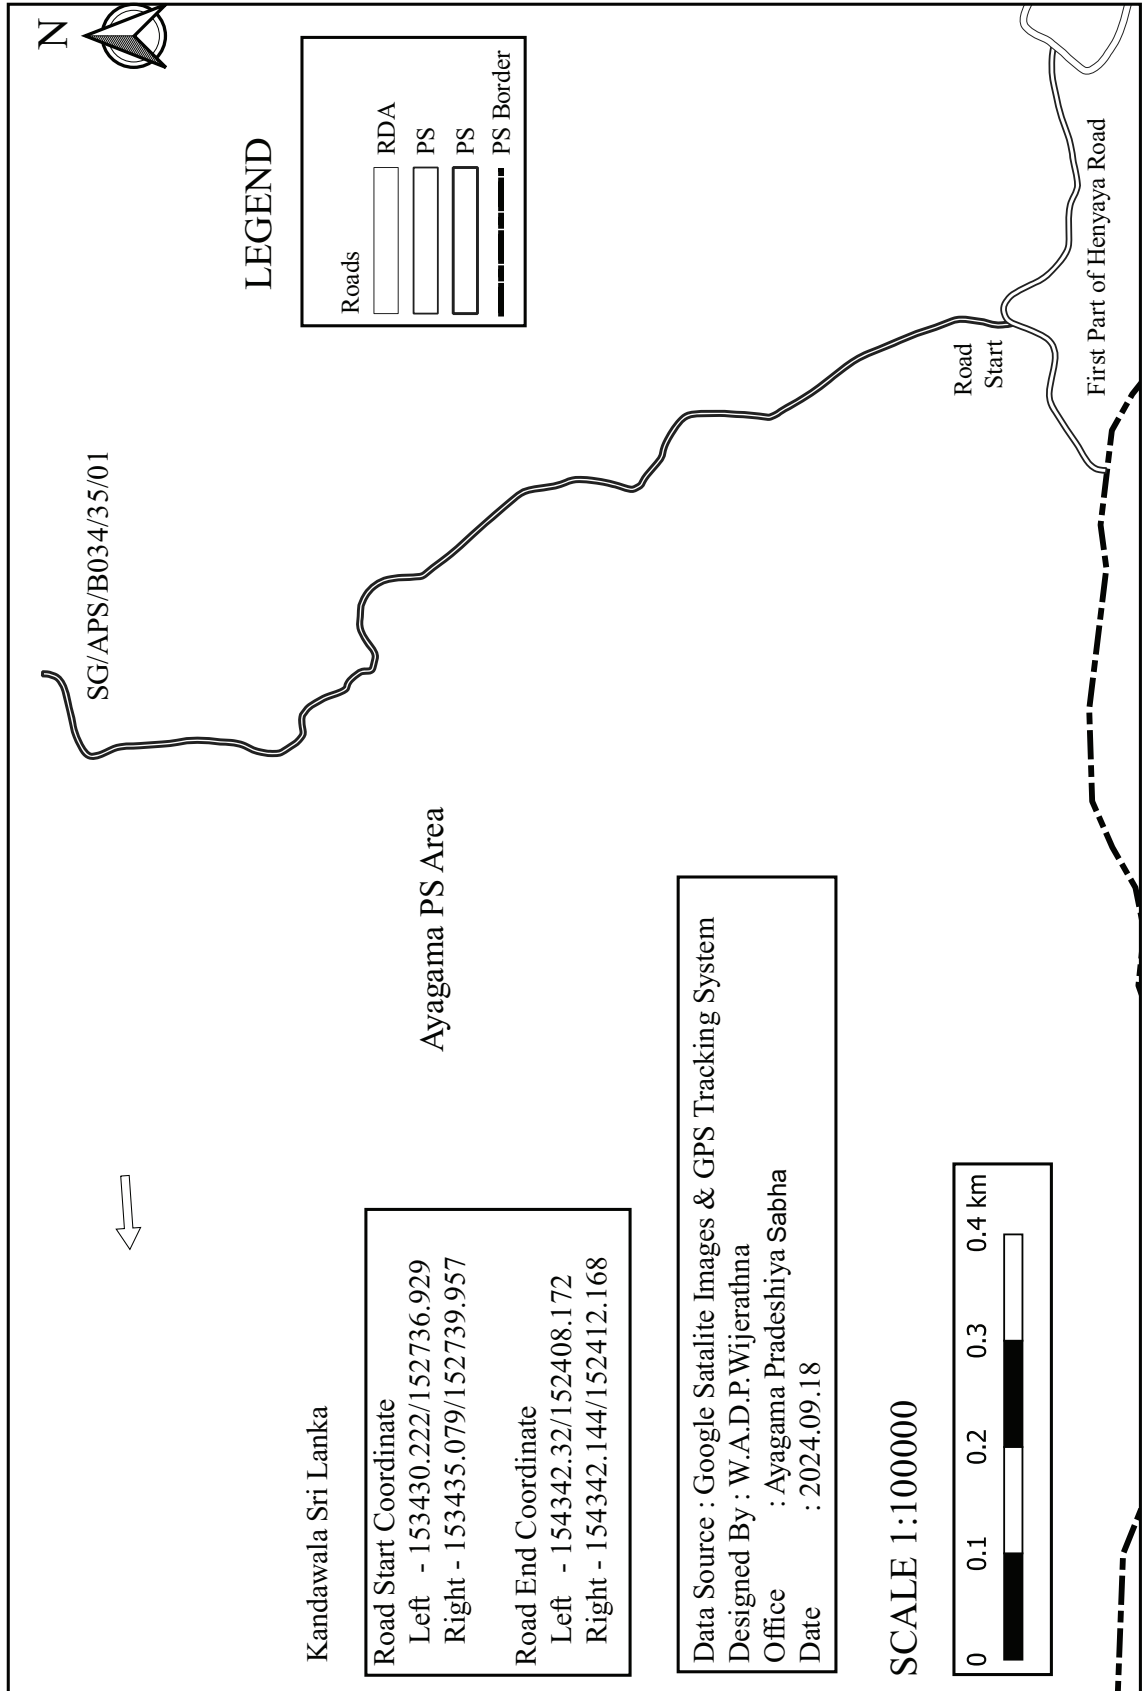


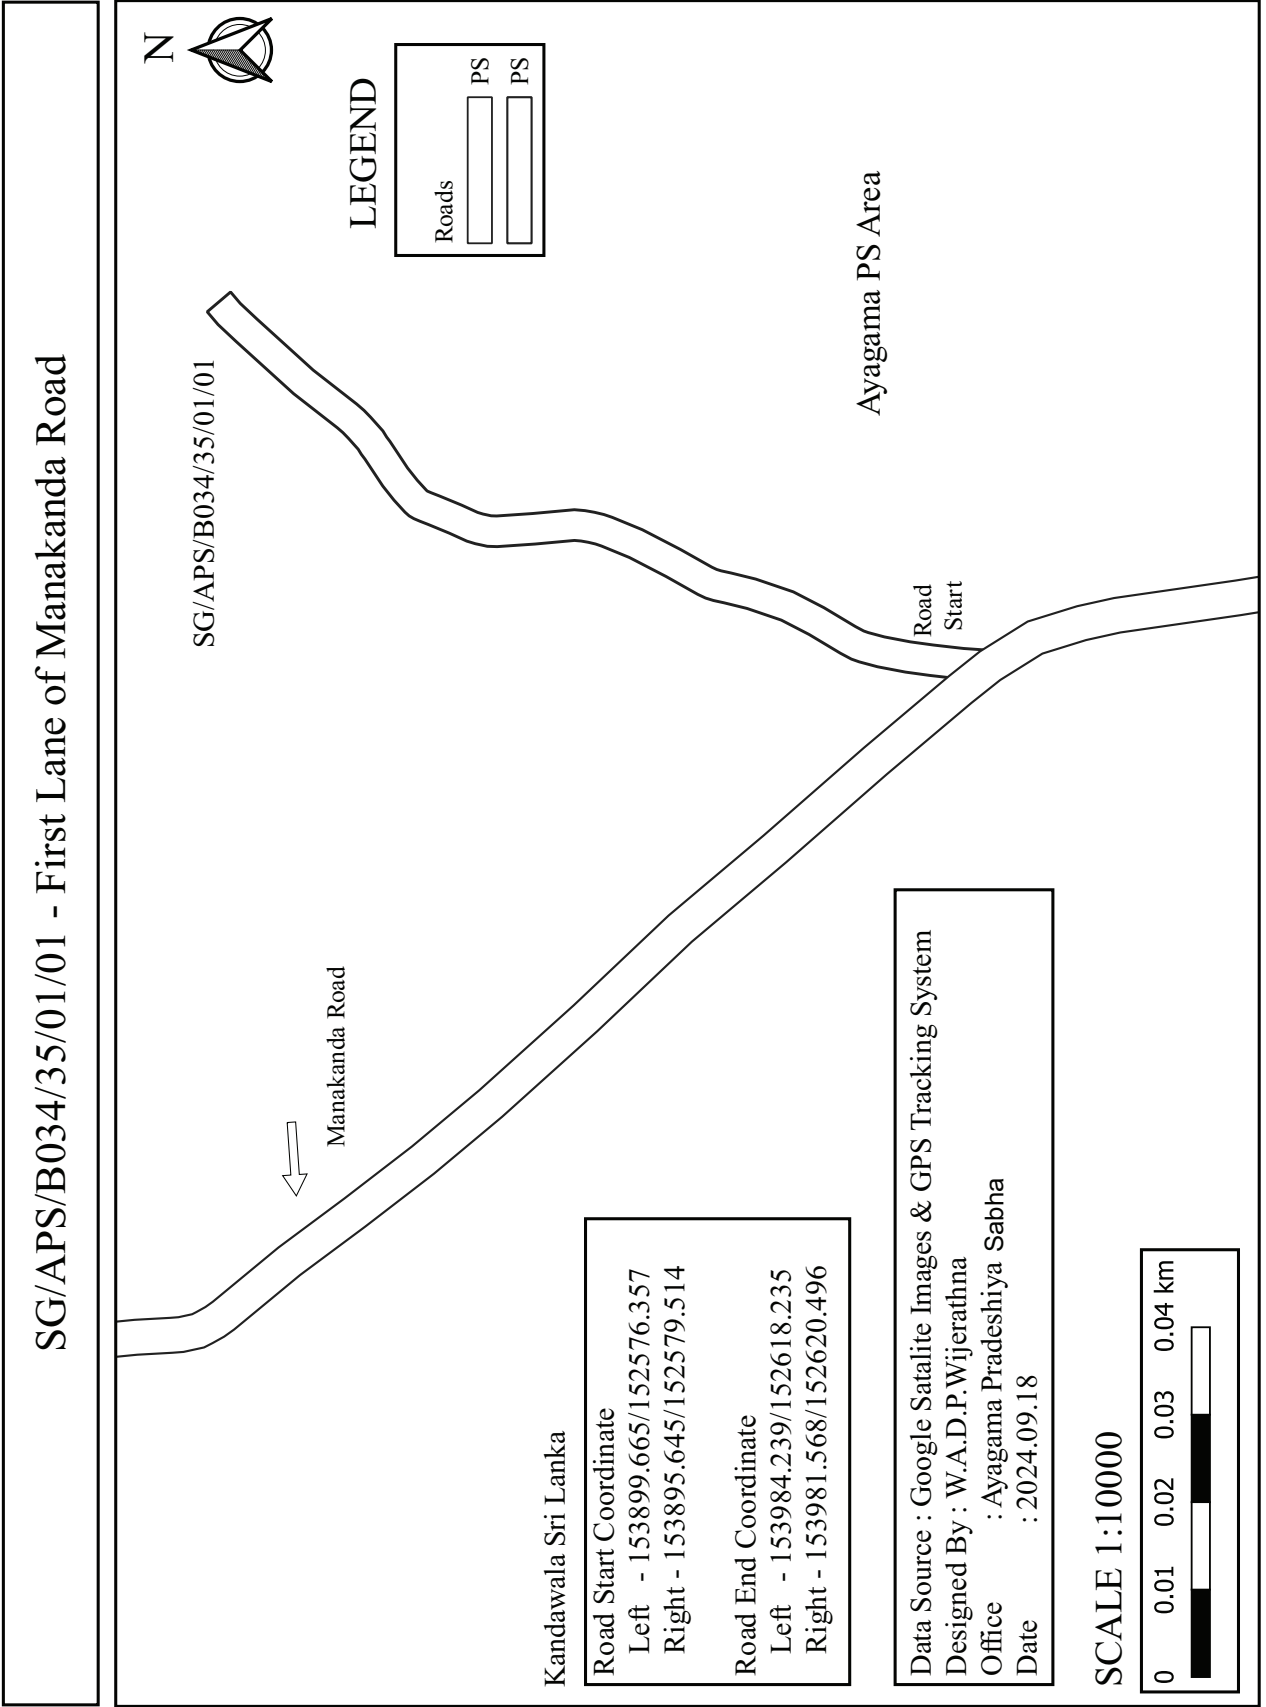


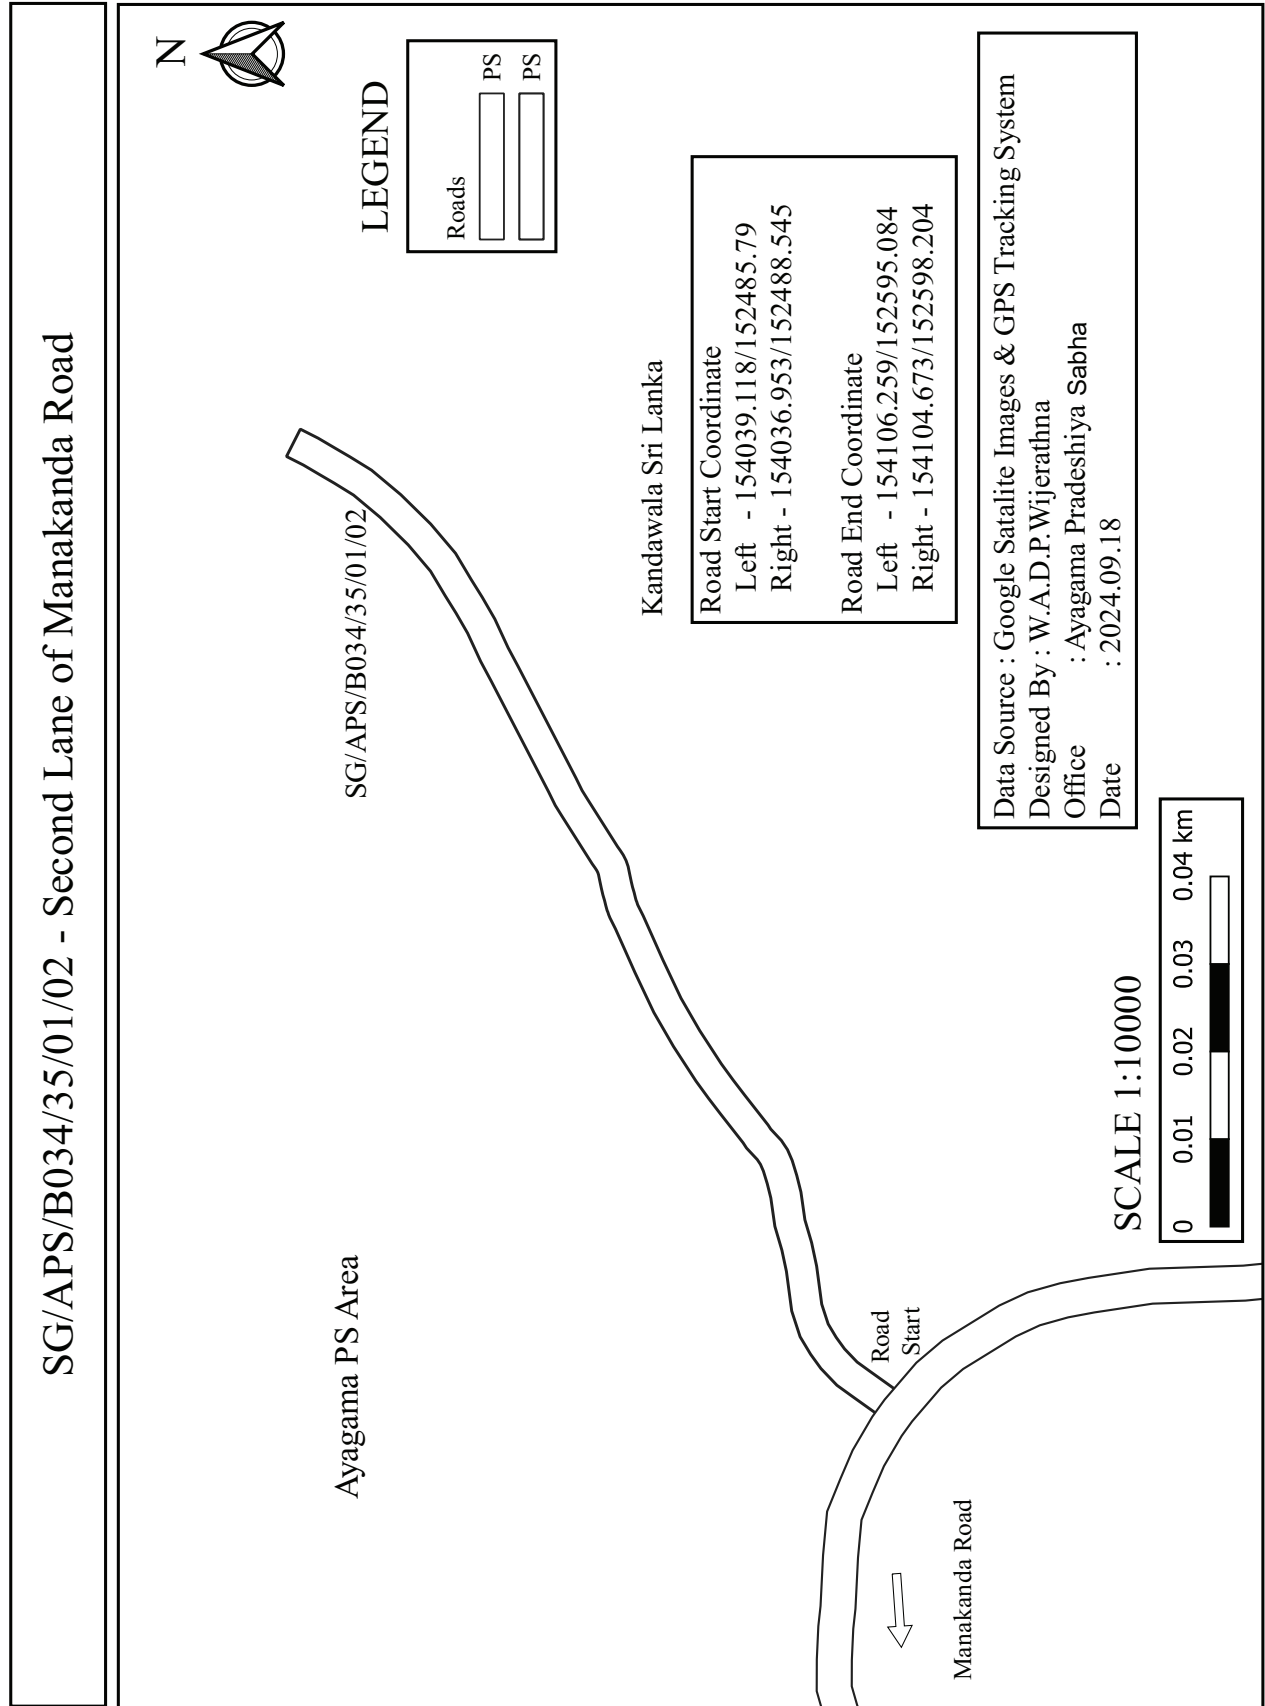

SG/APS/B034/35/01/03 - Third Lane of Manakanda Road

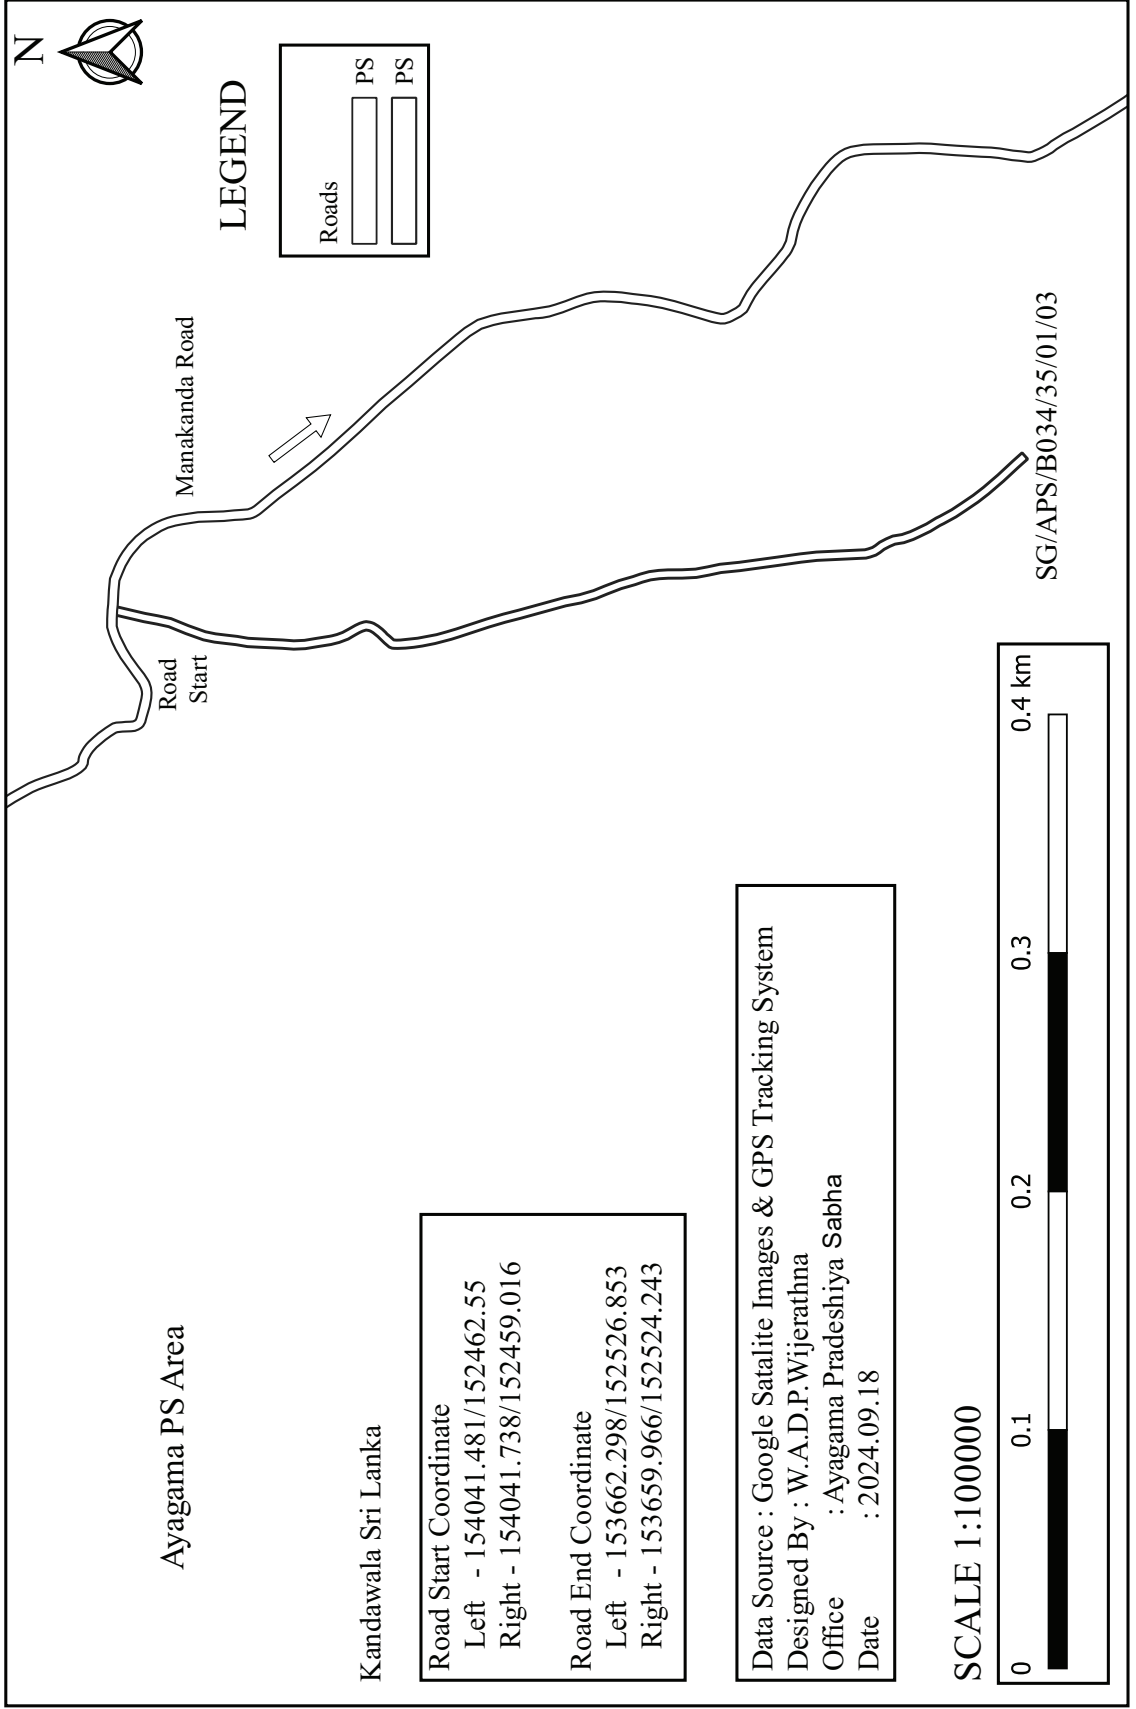

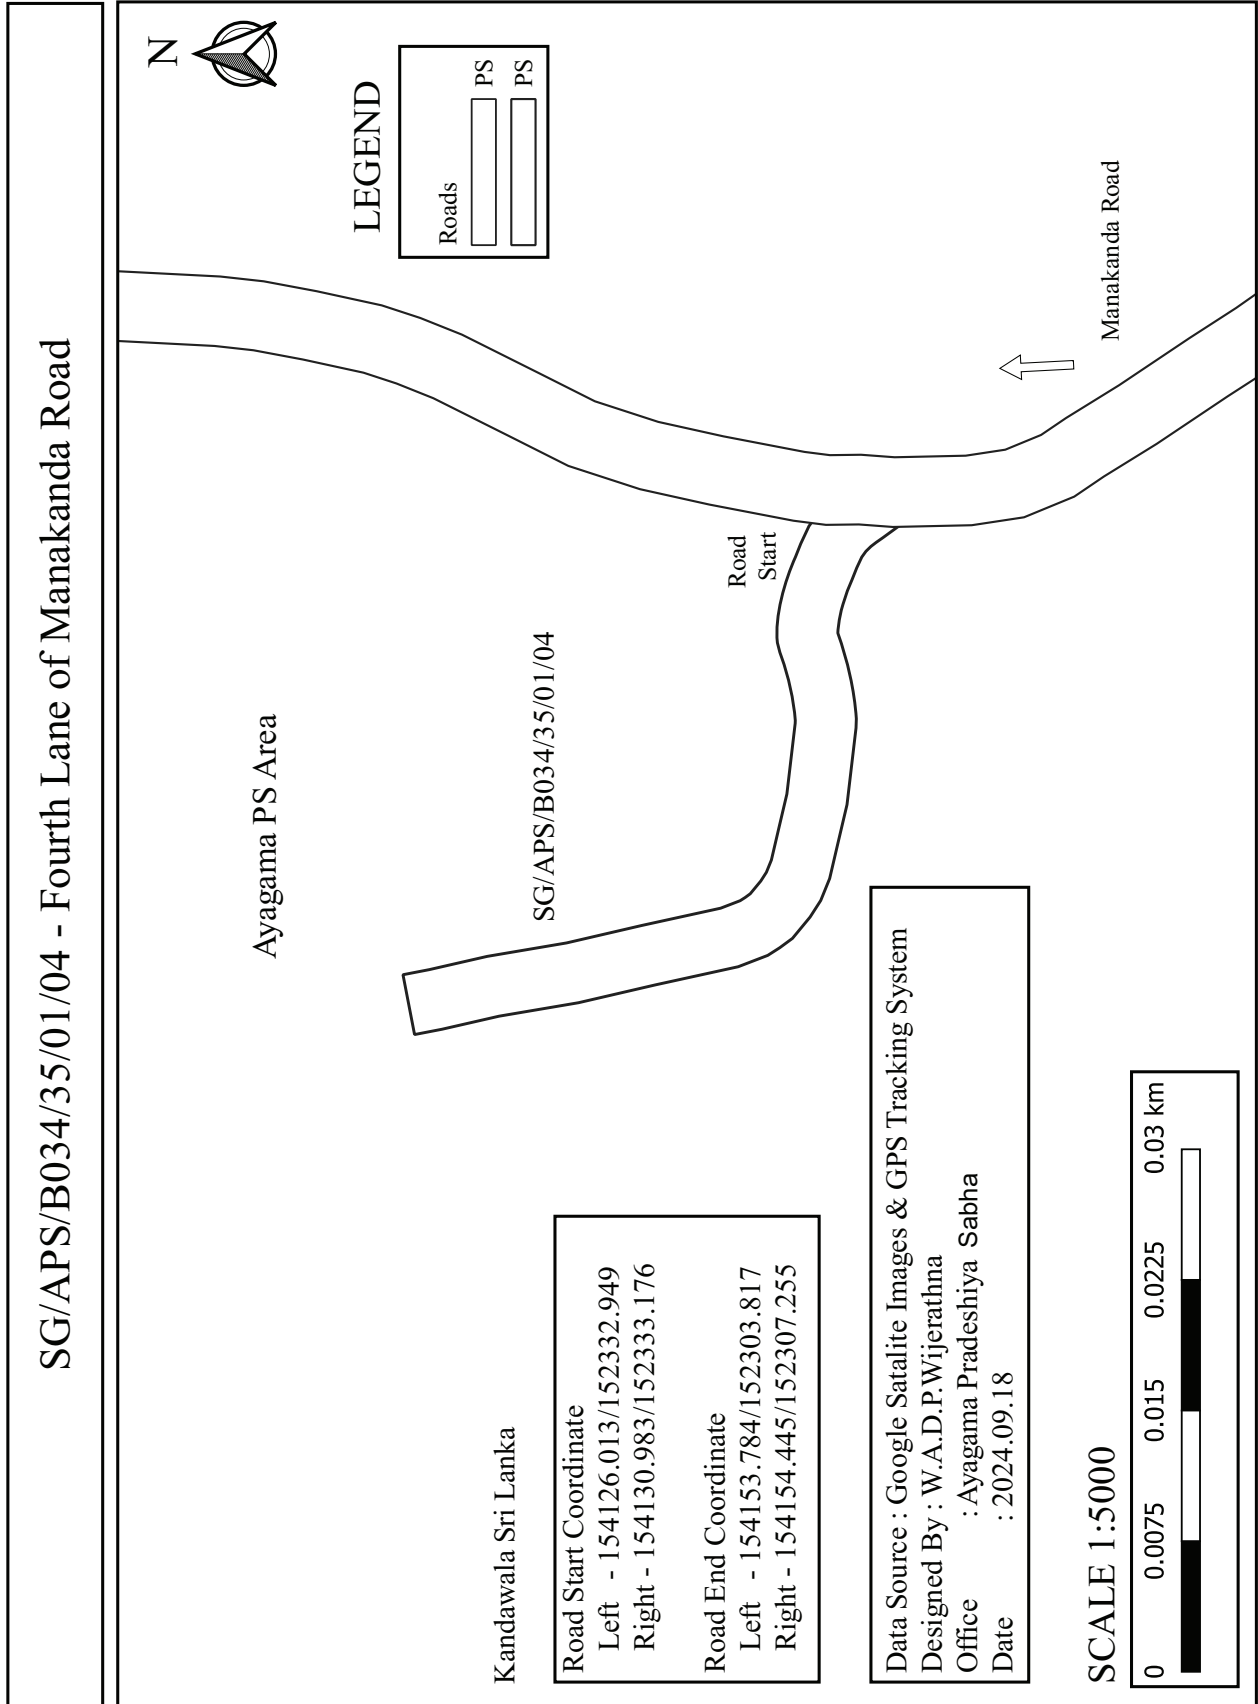

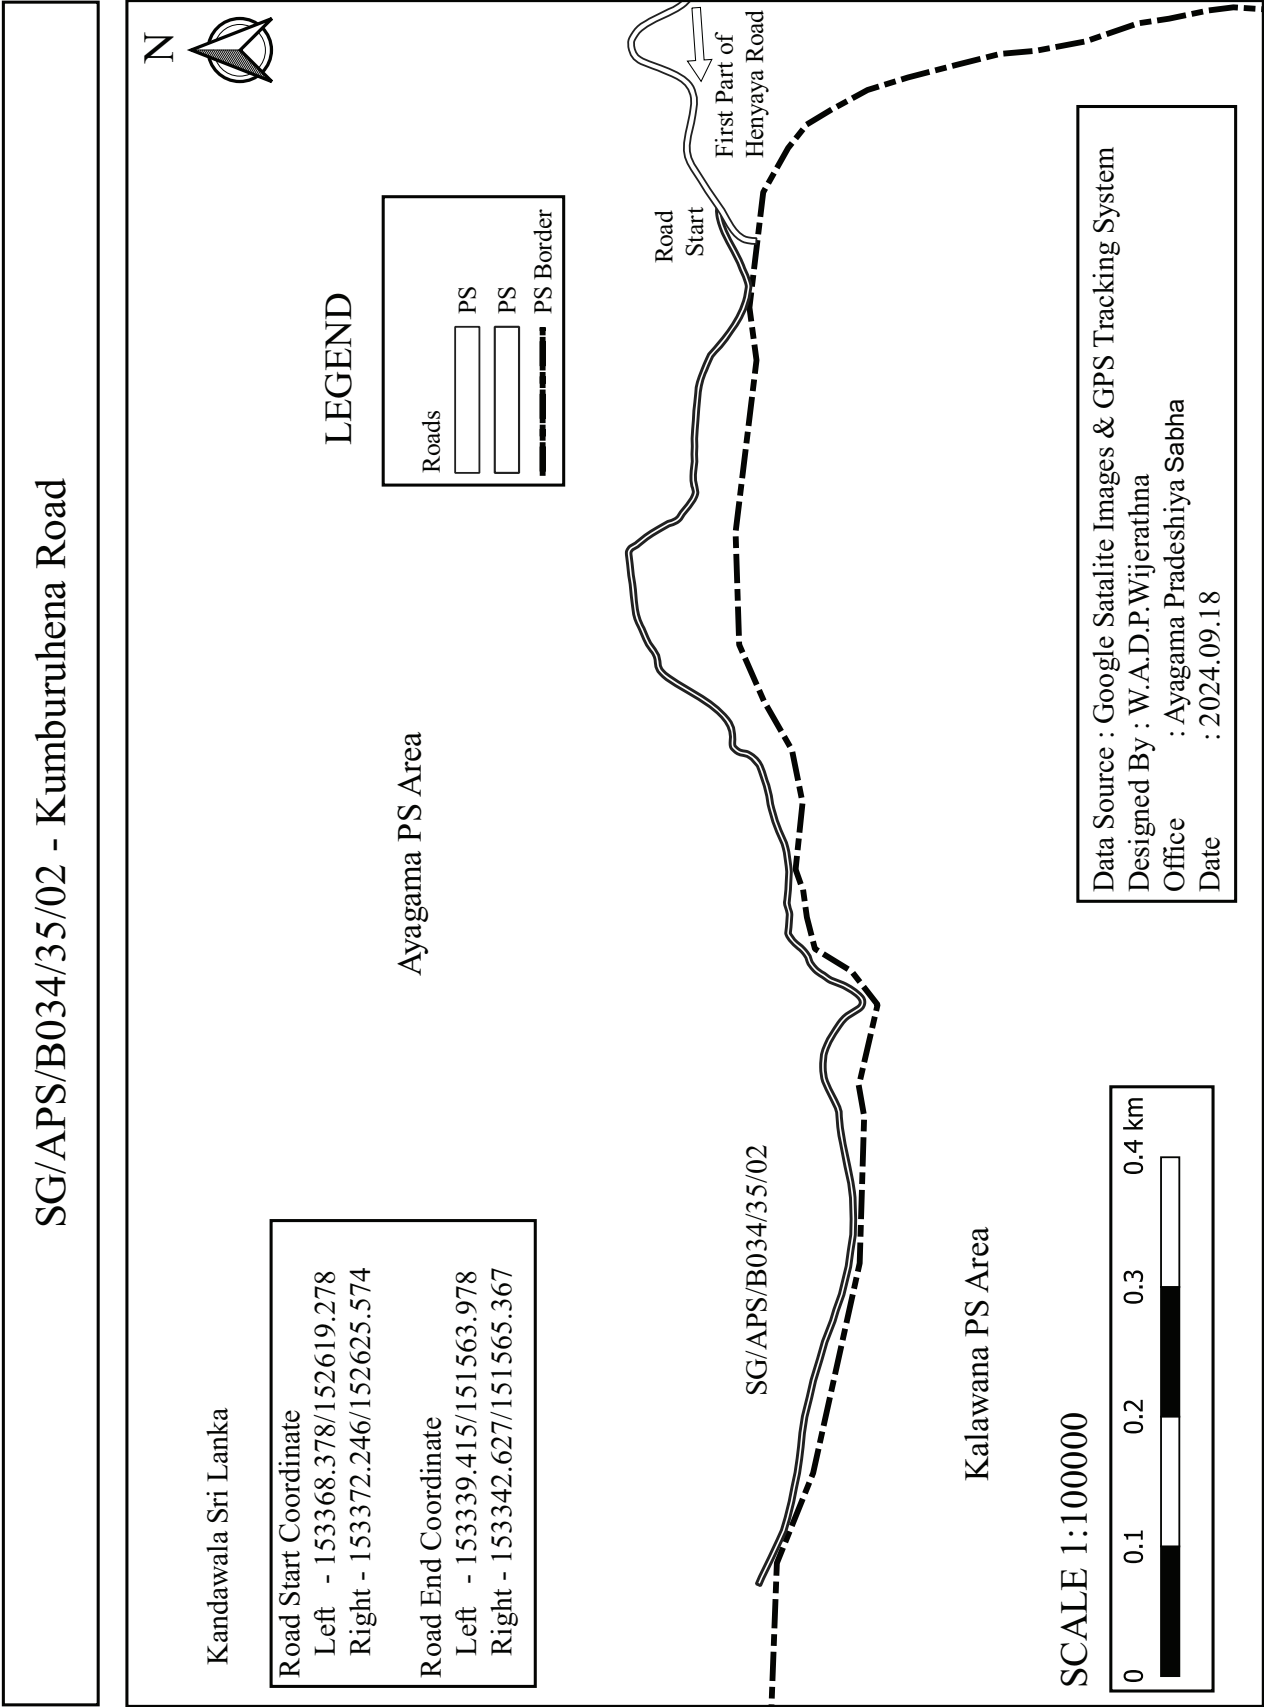

N

First Part of
Henyaya Road

Road
Start

SG/APS/B034/35/02

Kalawana PS Area

Ayagama PS Area

SCALE 1:100000

0
0.4 km

0.1
0.3


0.2
0.4

Data Source : Google Satalite Images & GPS Tracking System


Designed By : W.A.D.P.Wijerathna


Office : Ayagama Pradeshiya Sabha


Date : 2024.09.18

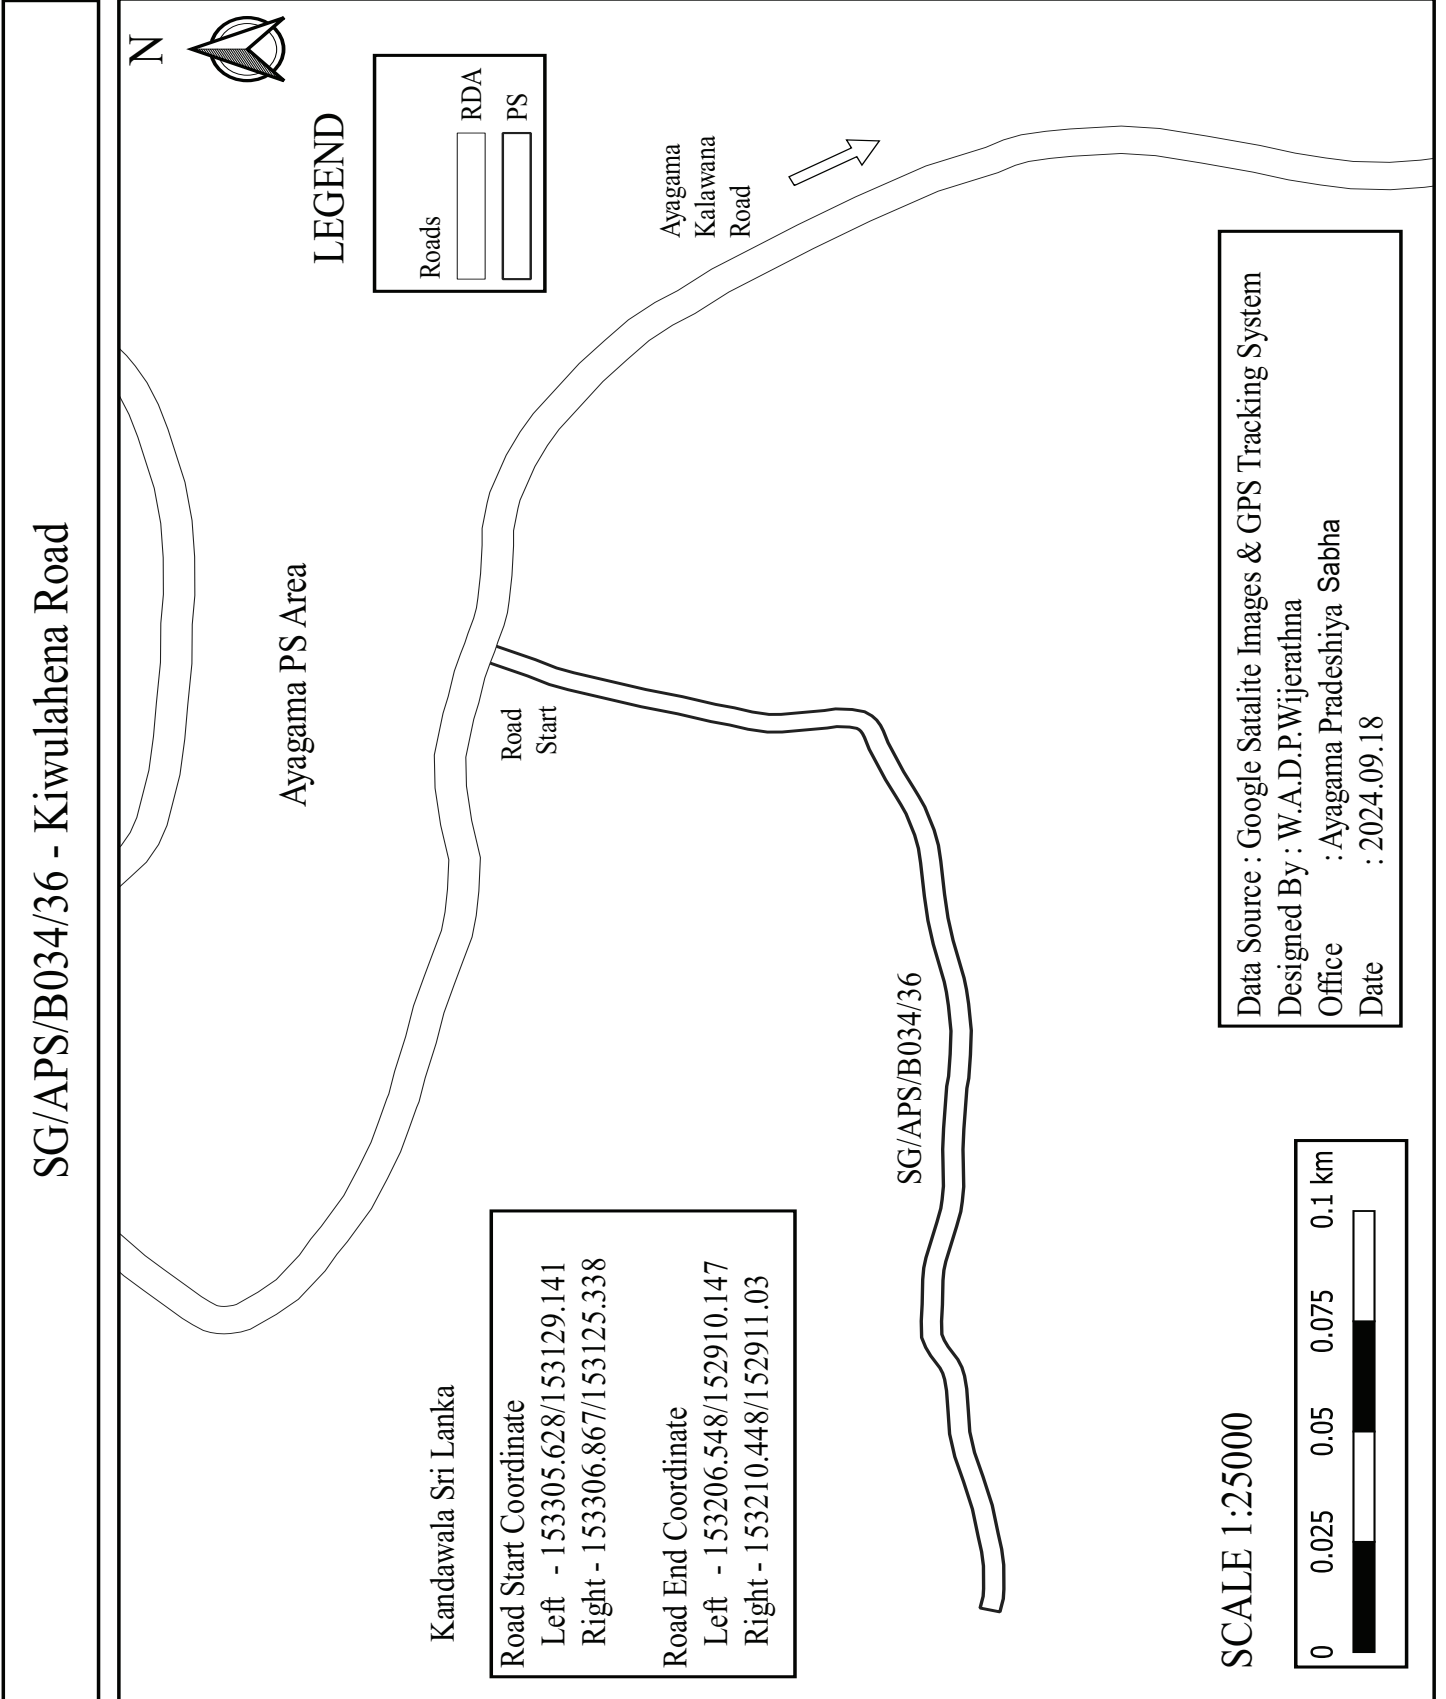



SG/APS/B034/37 - Kandaweldola Road

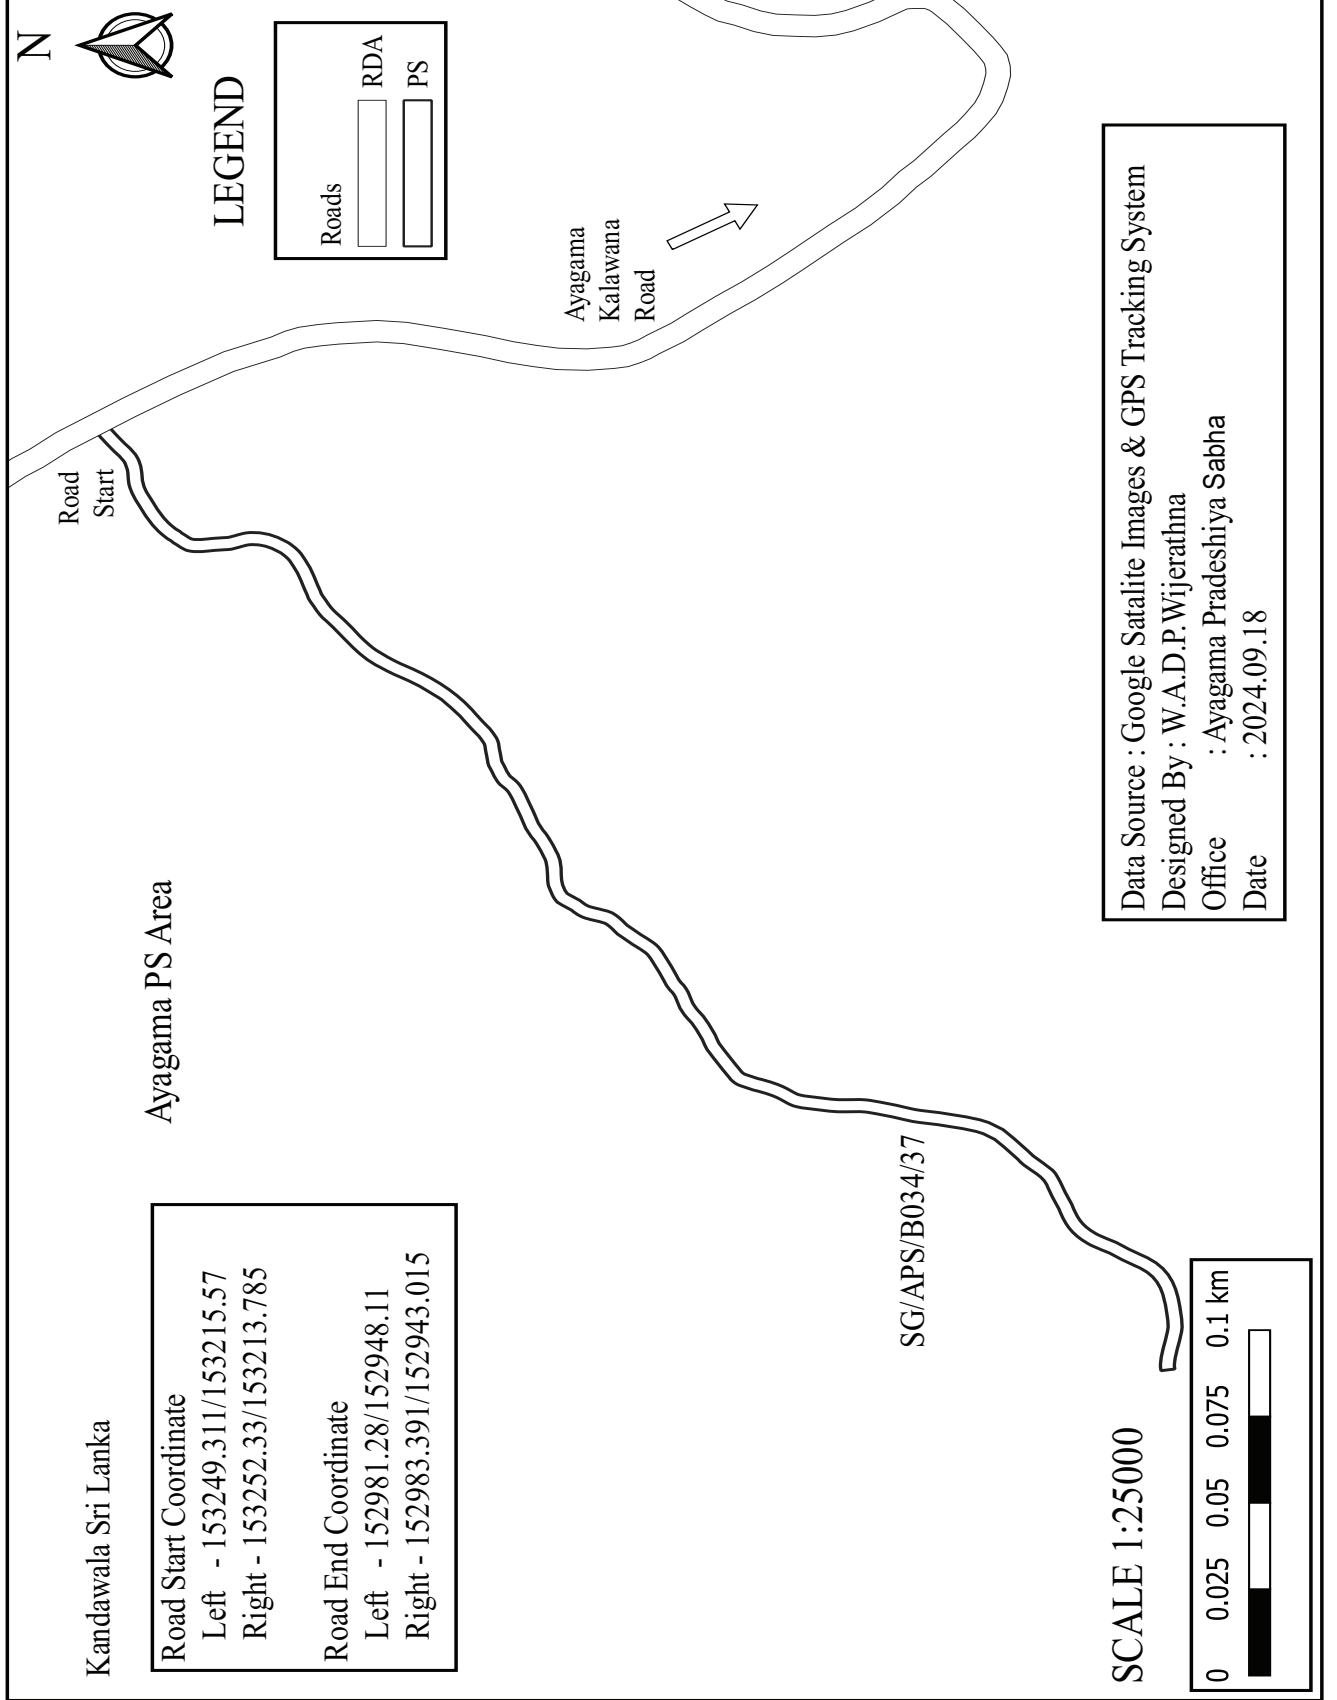


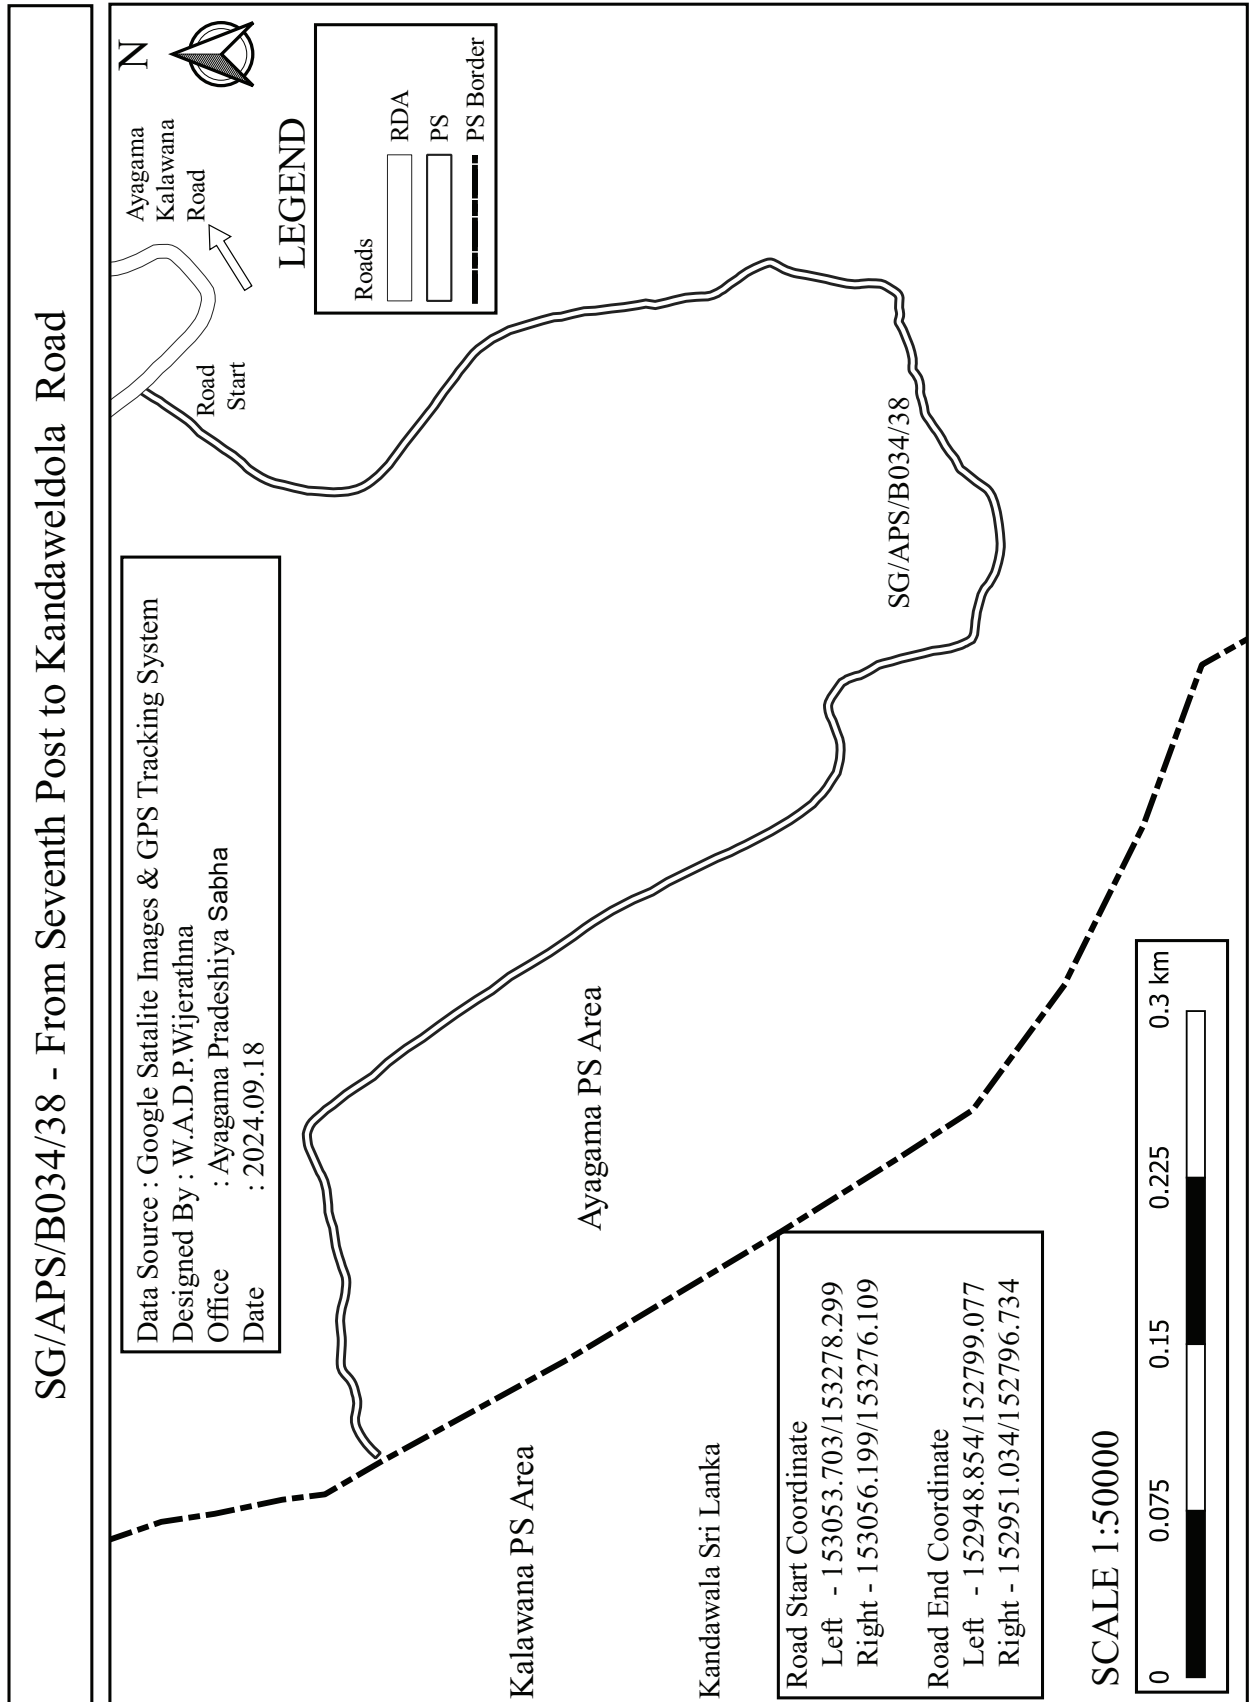


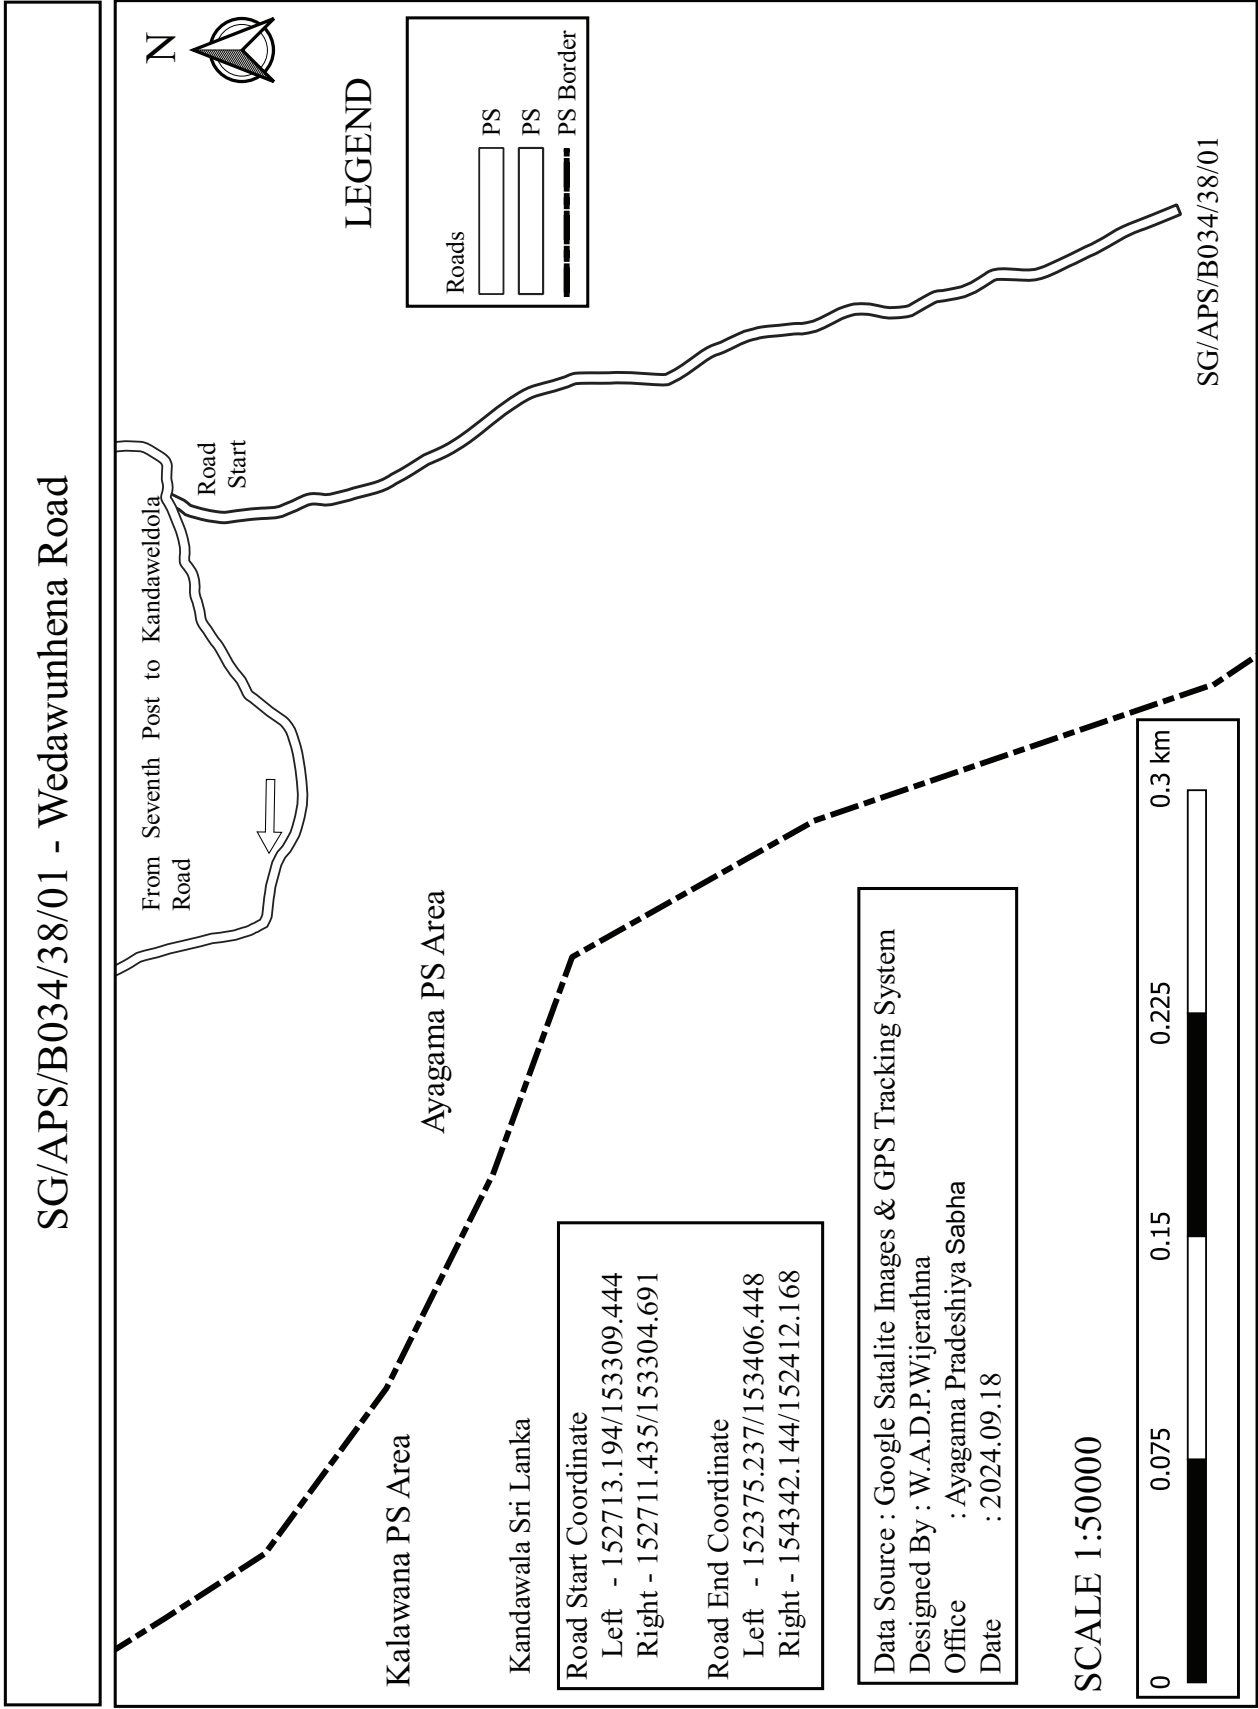


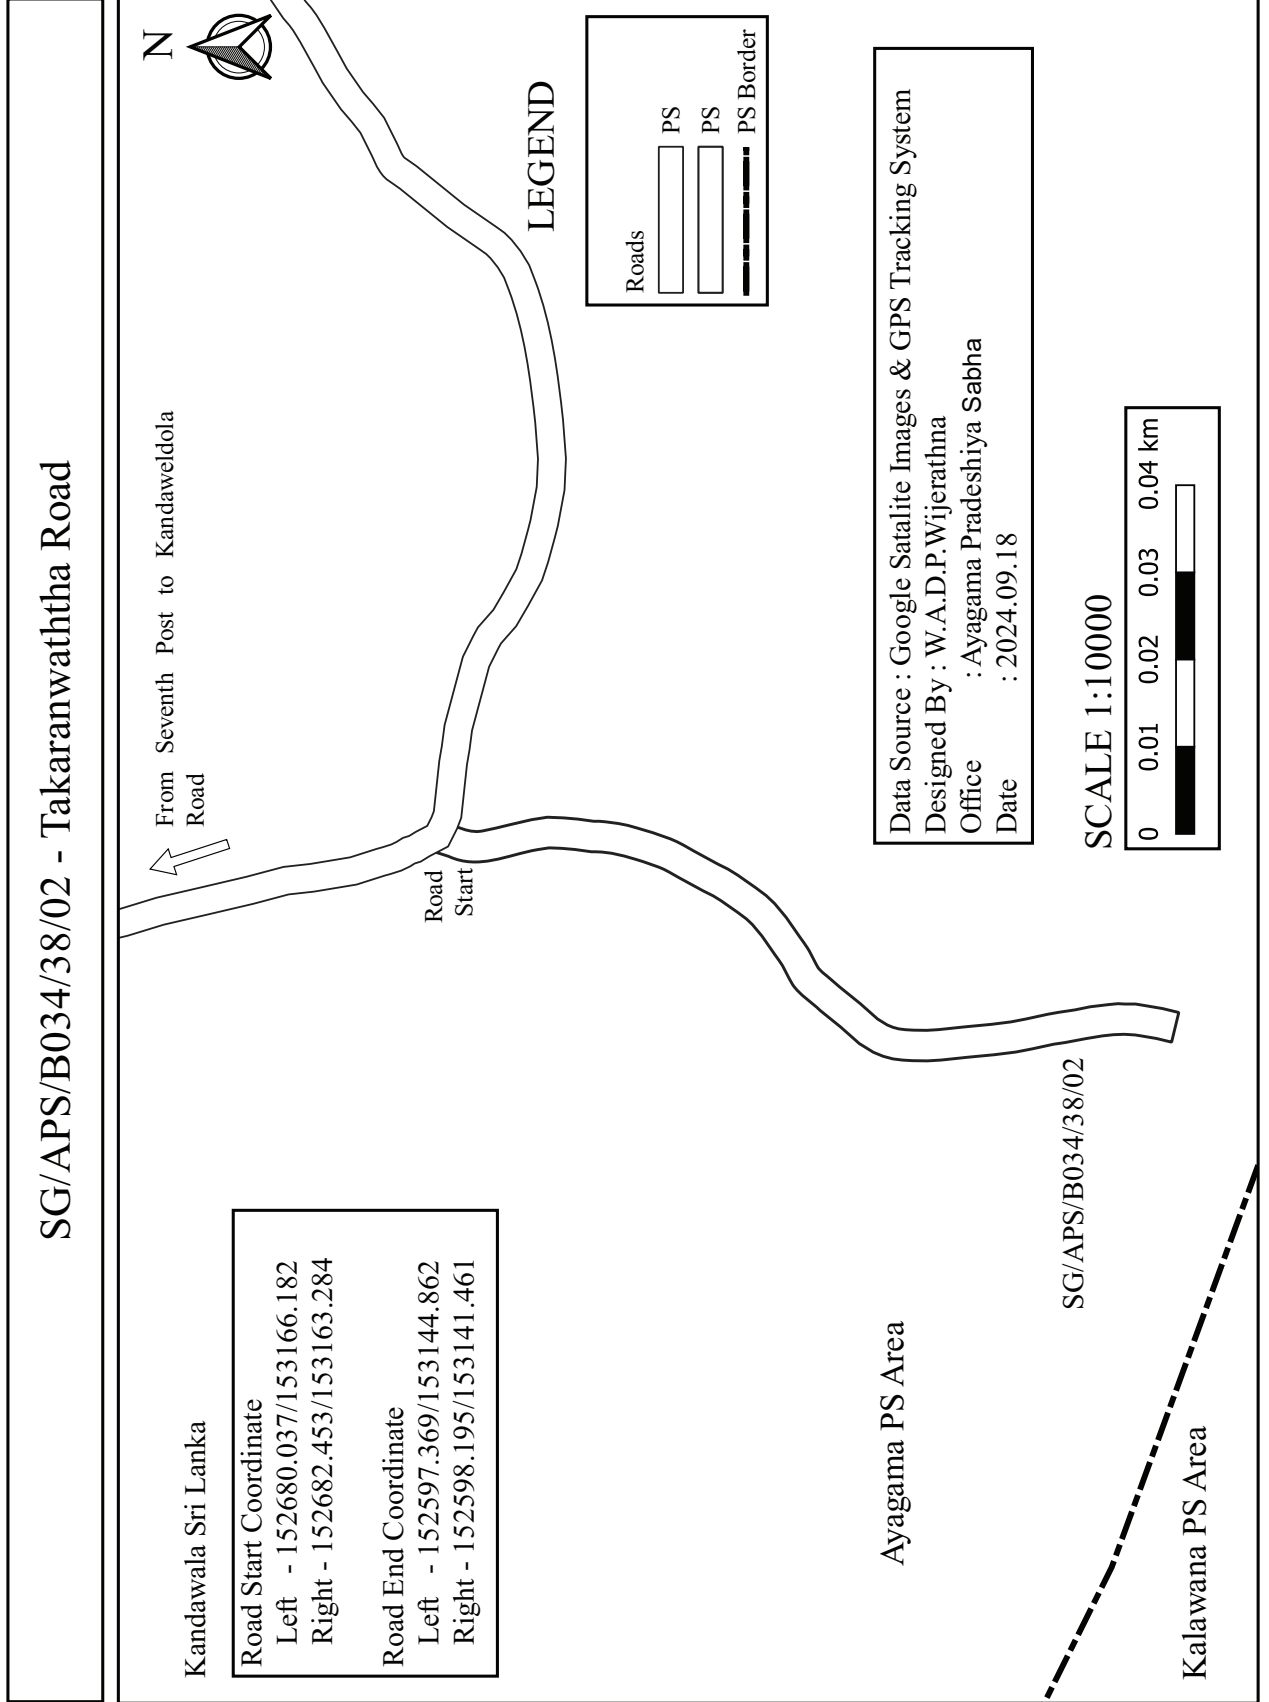


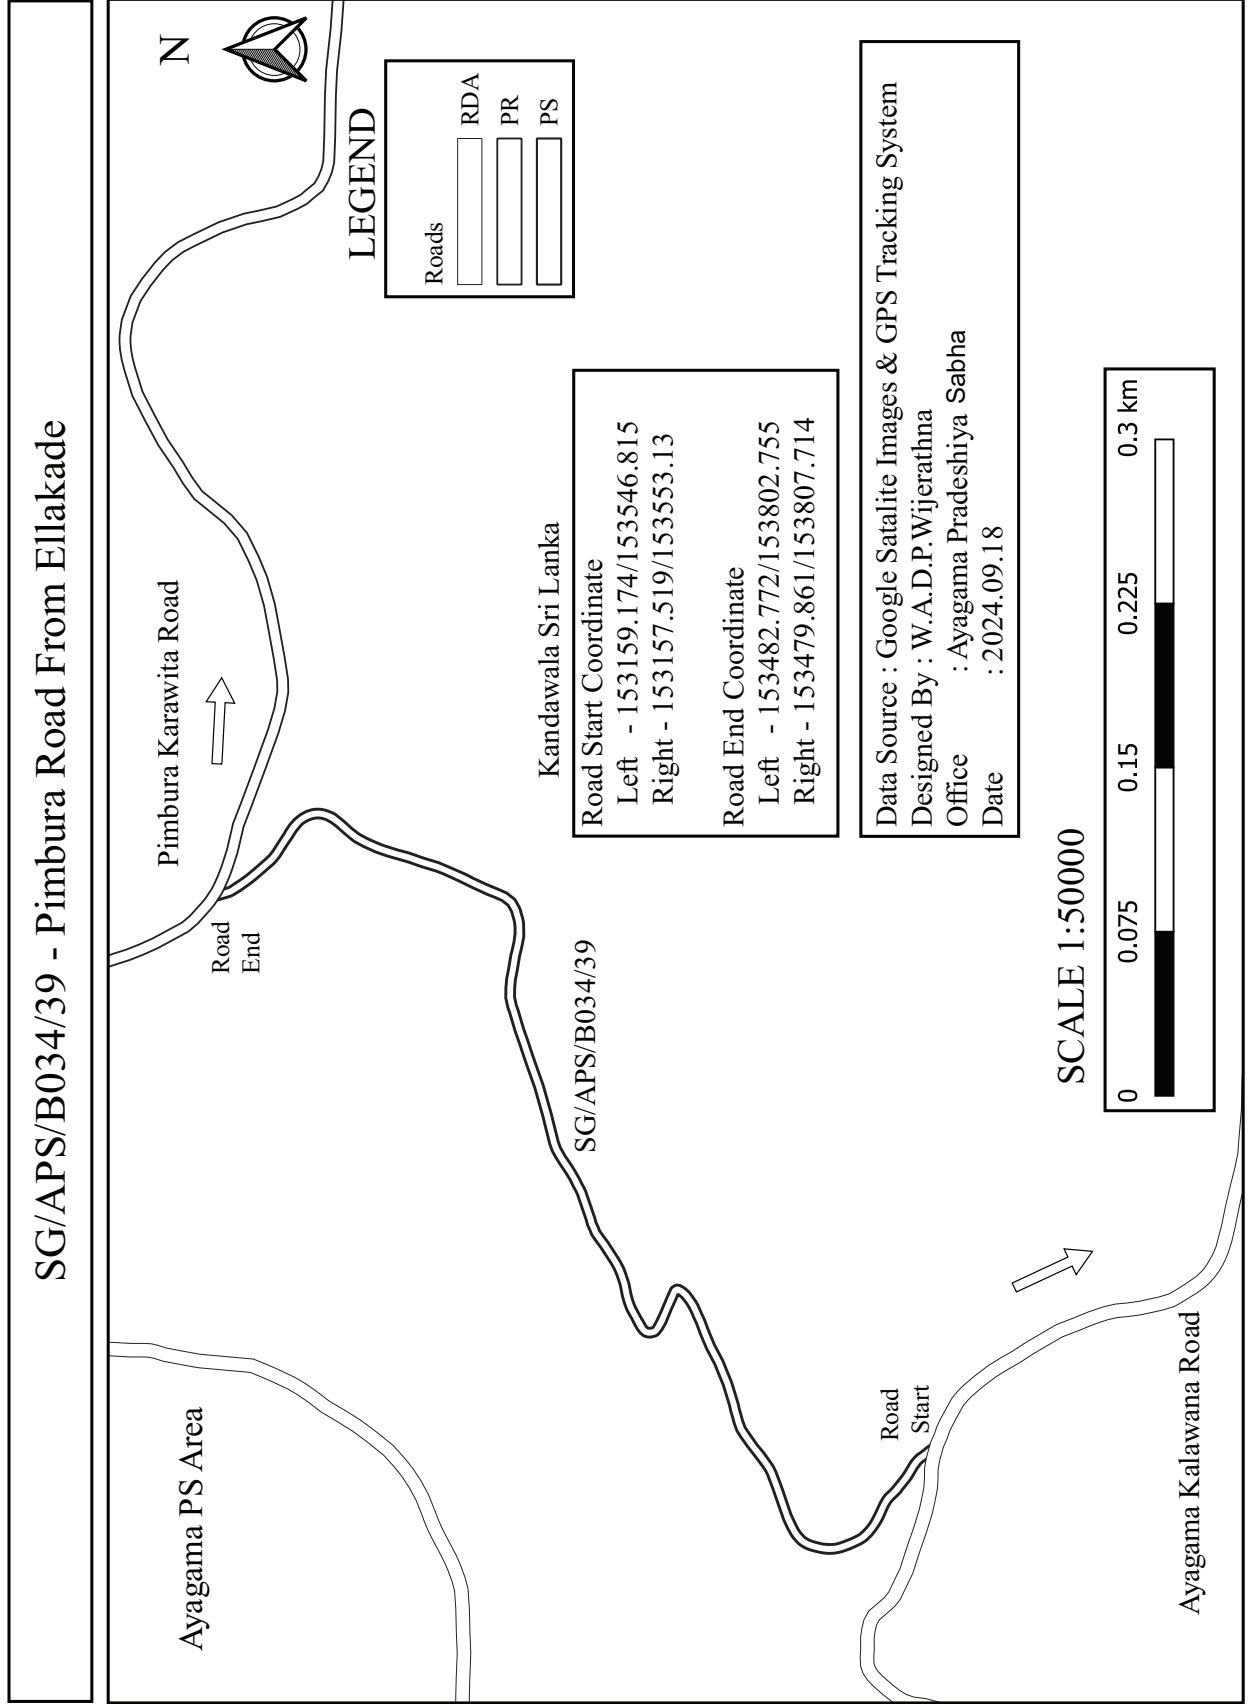


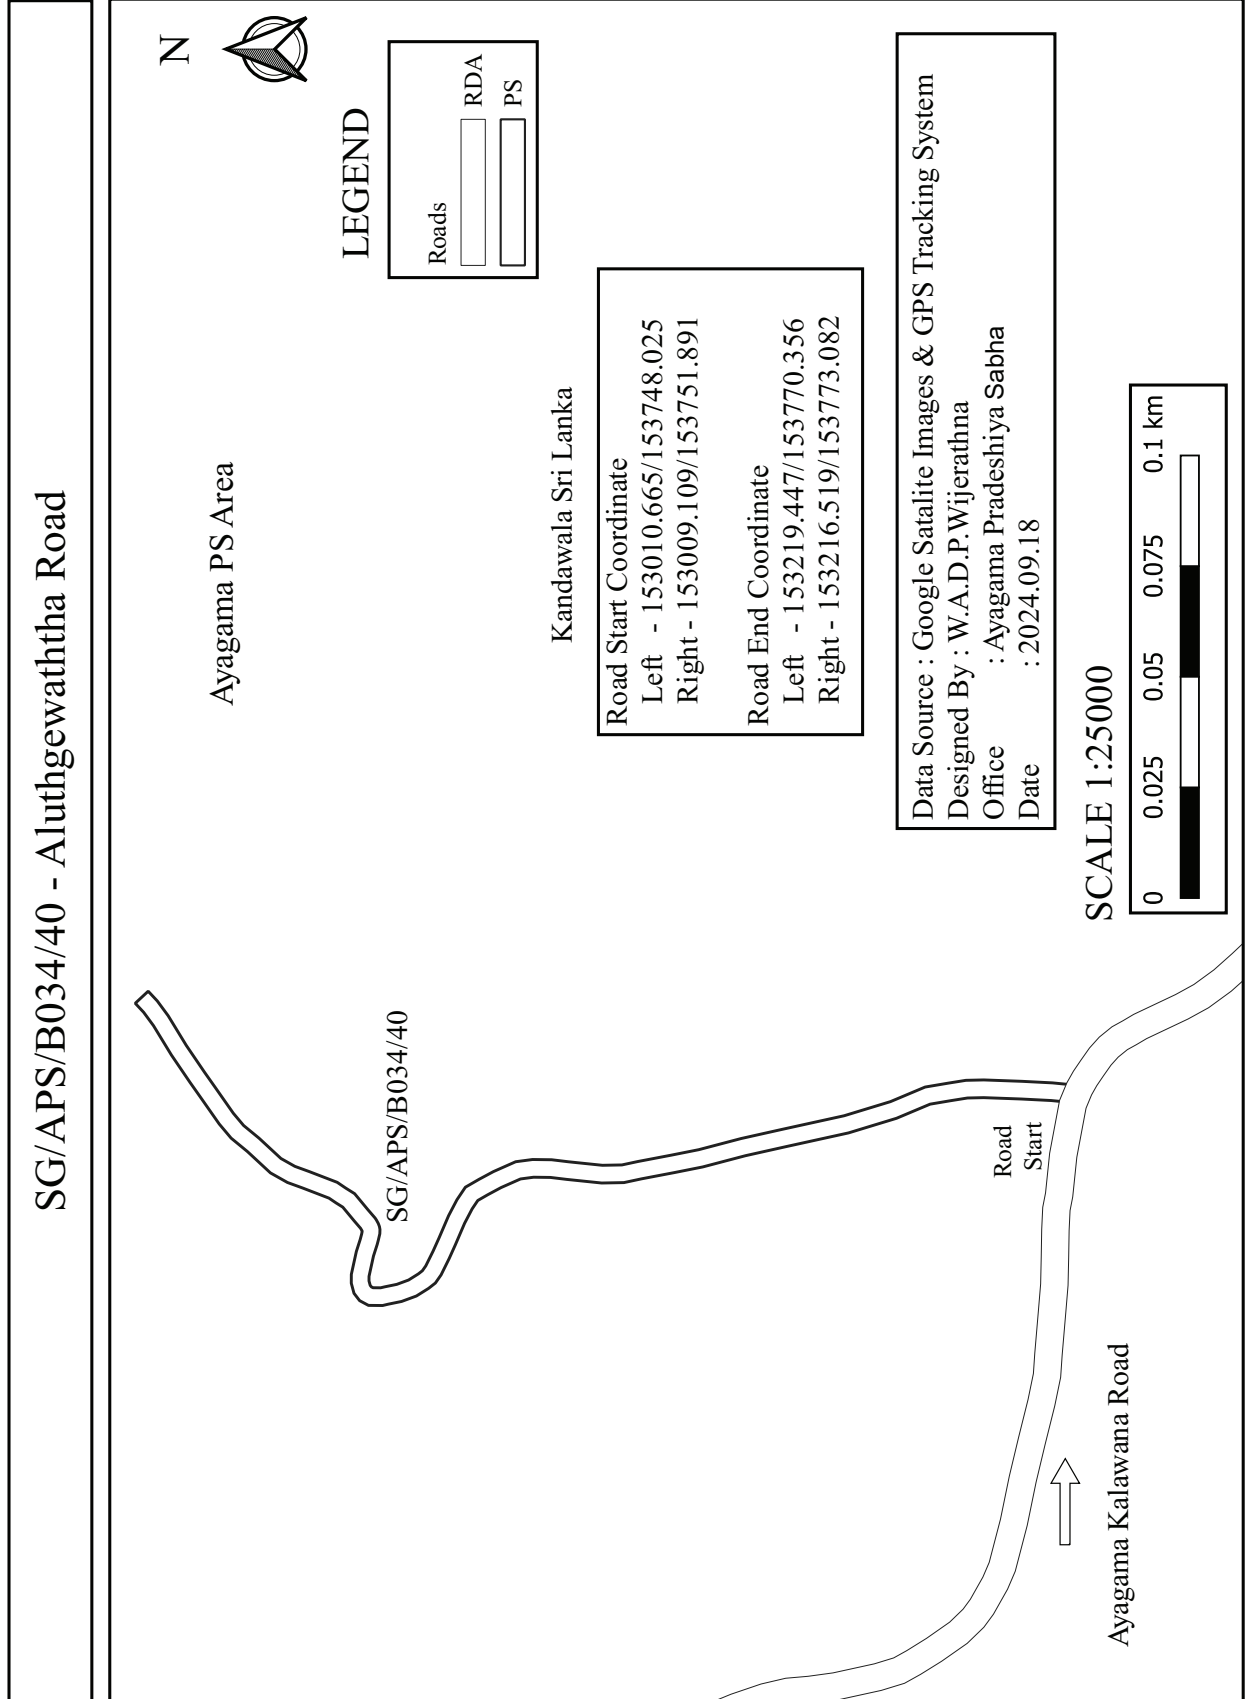


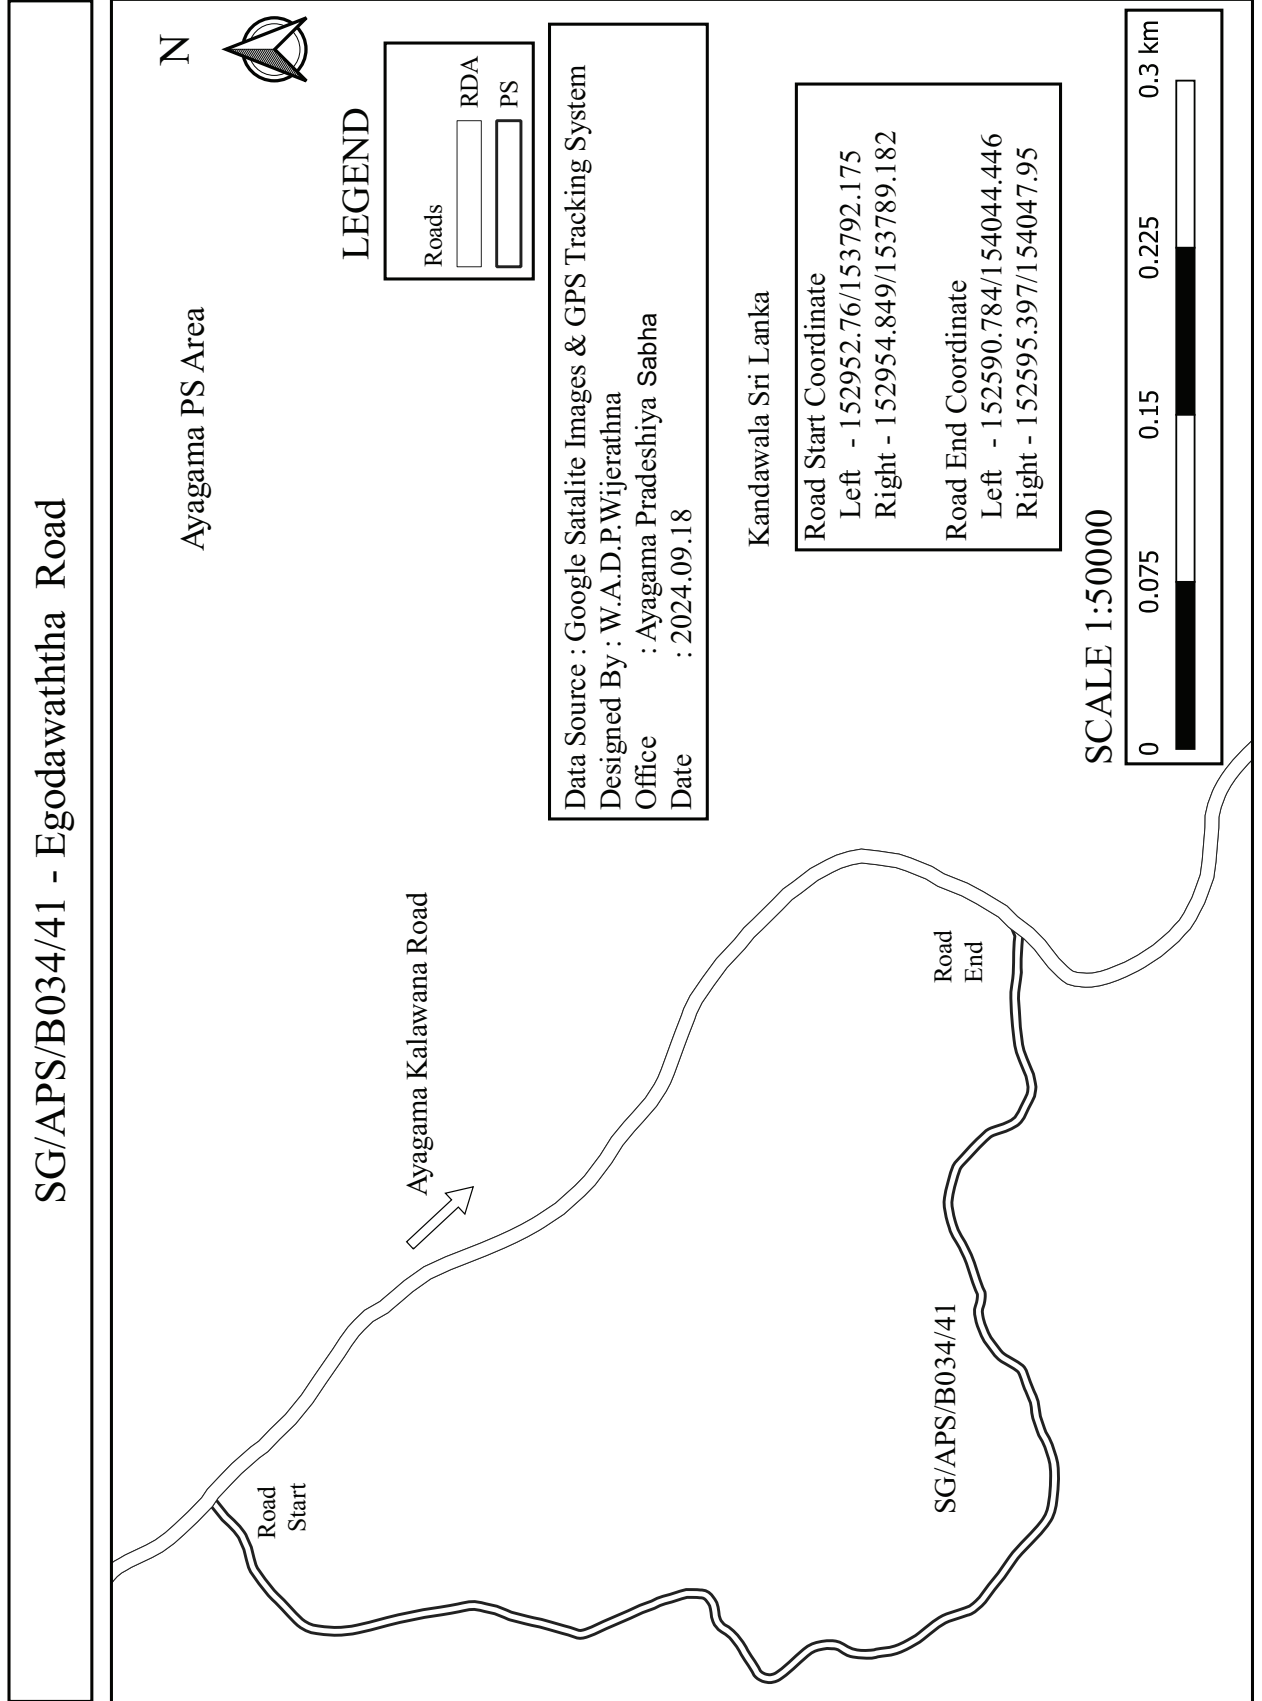


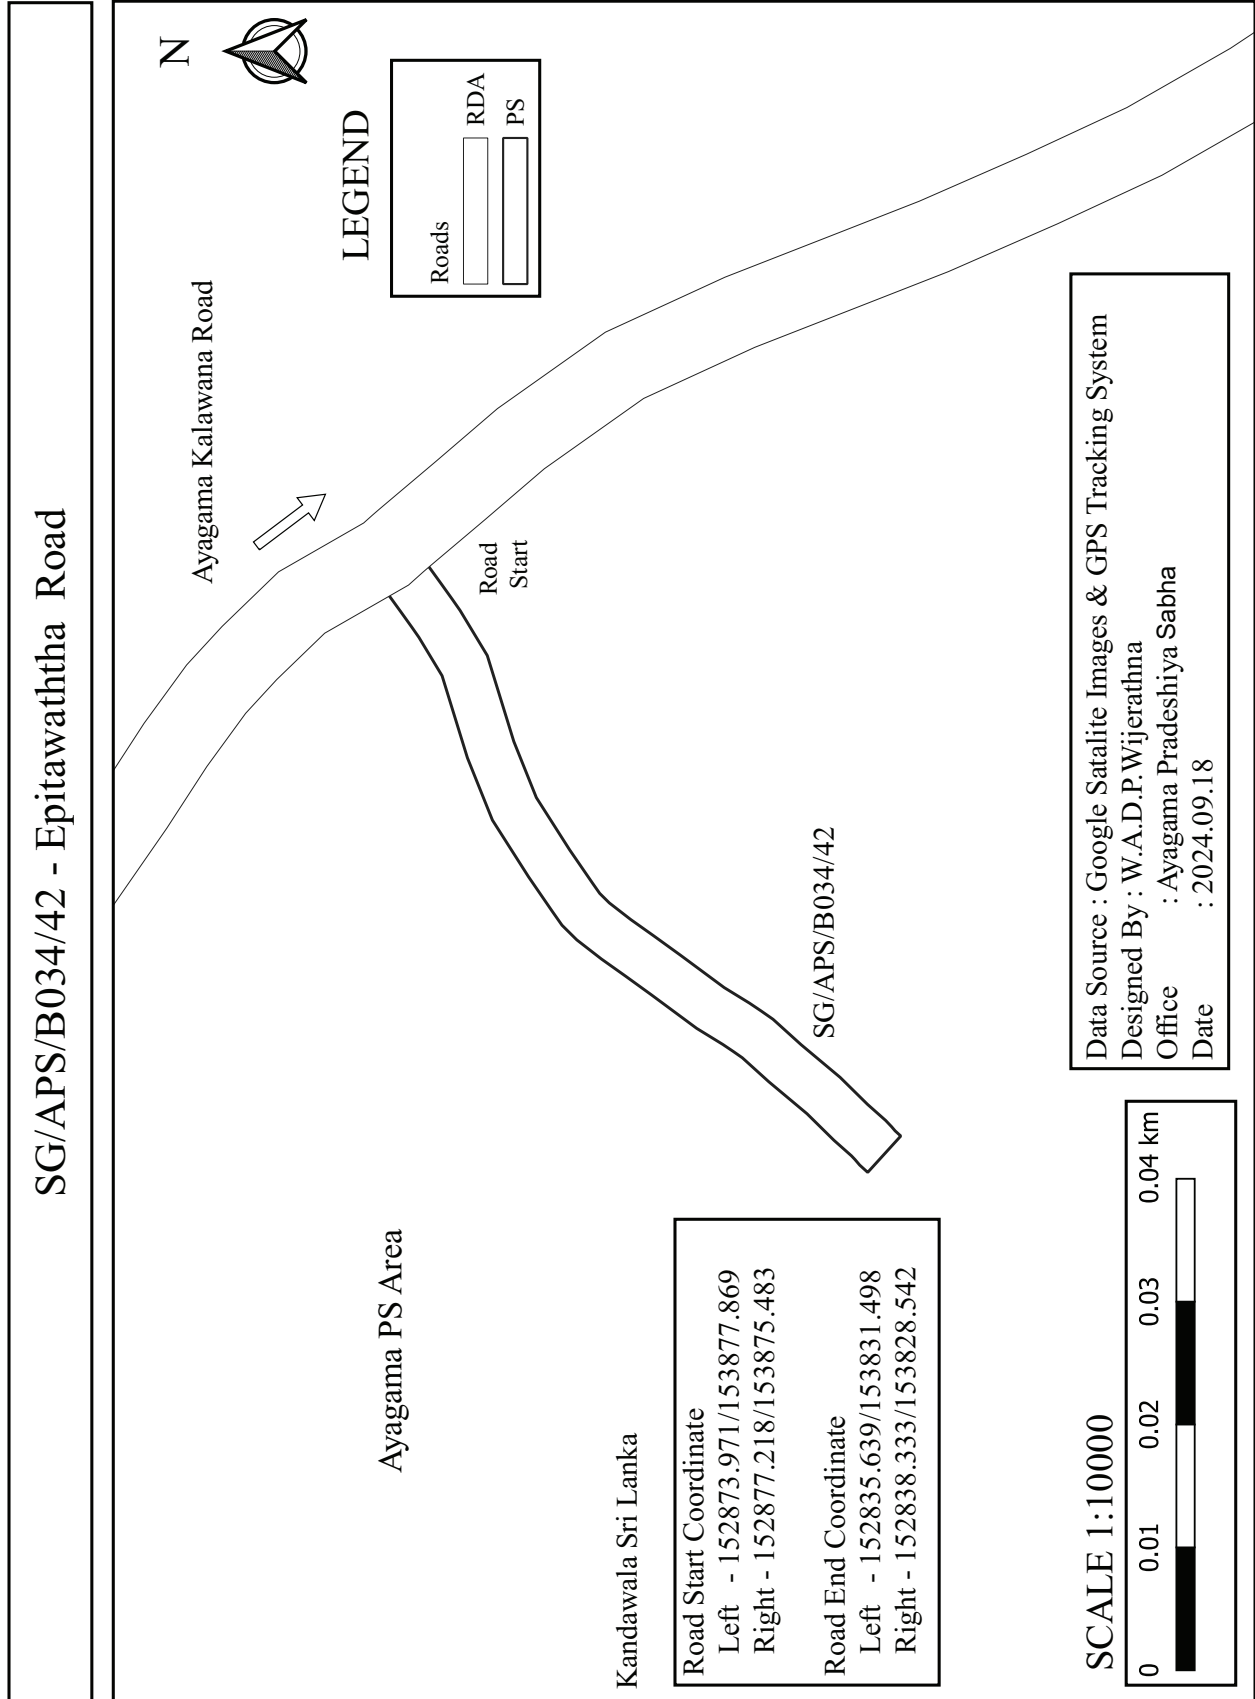


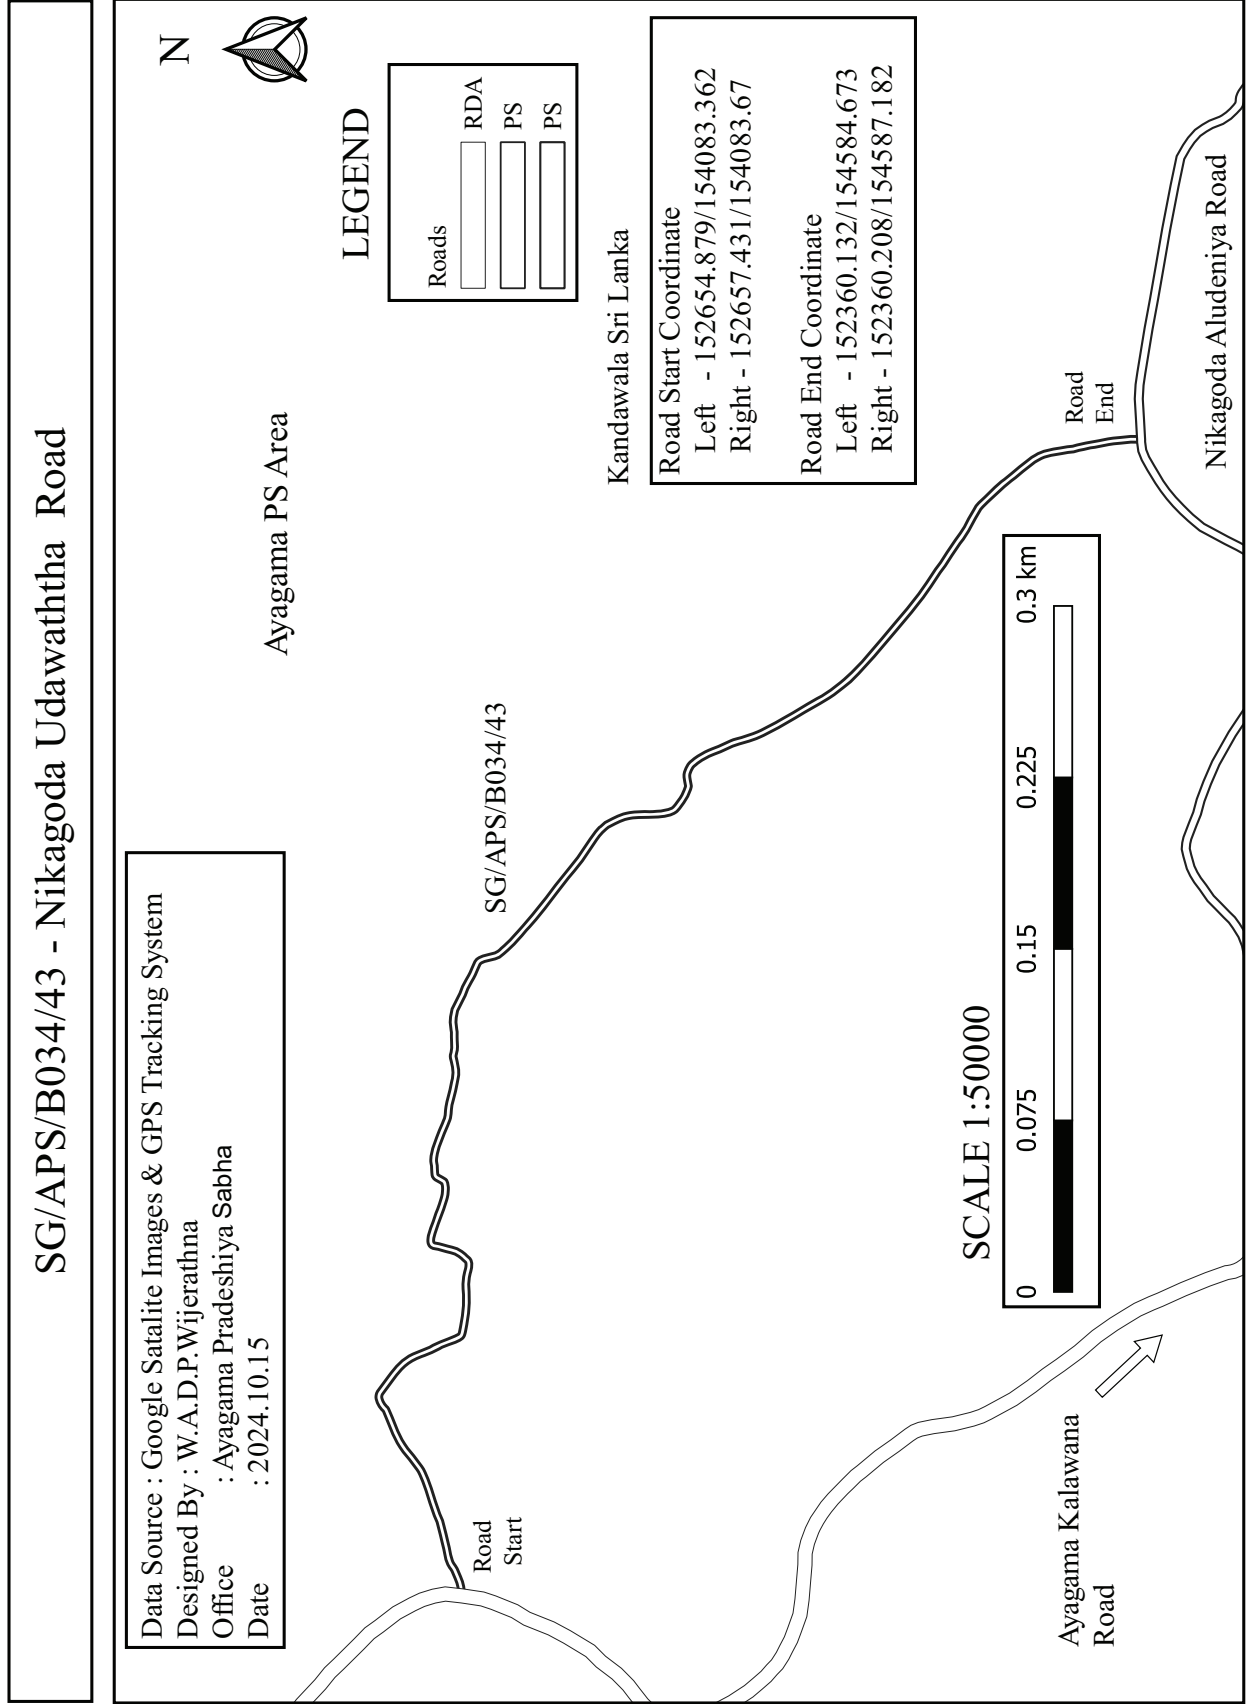


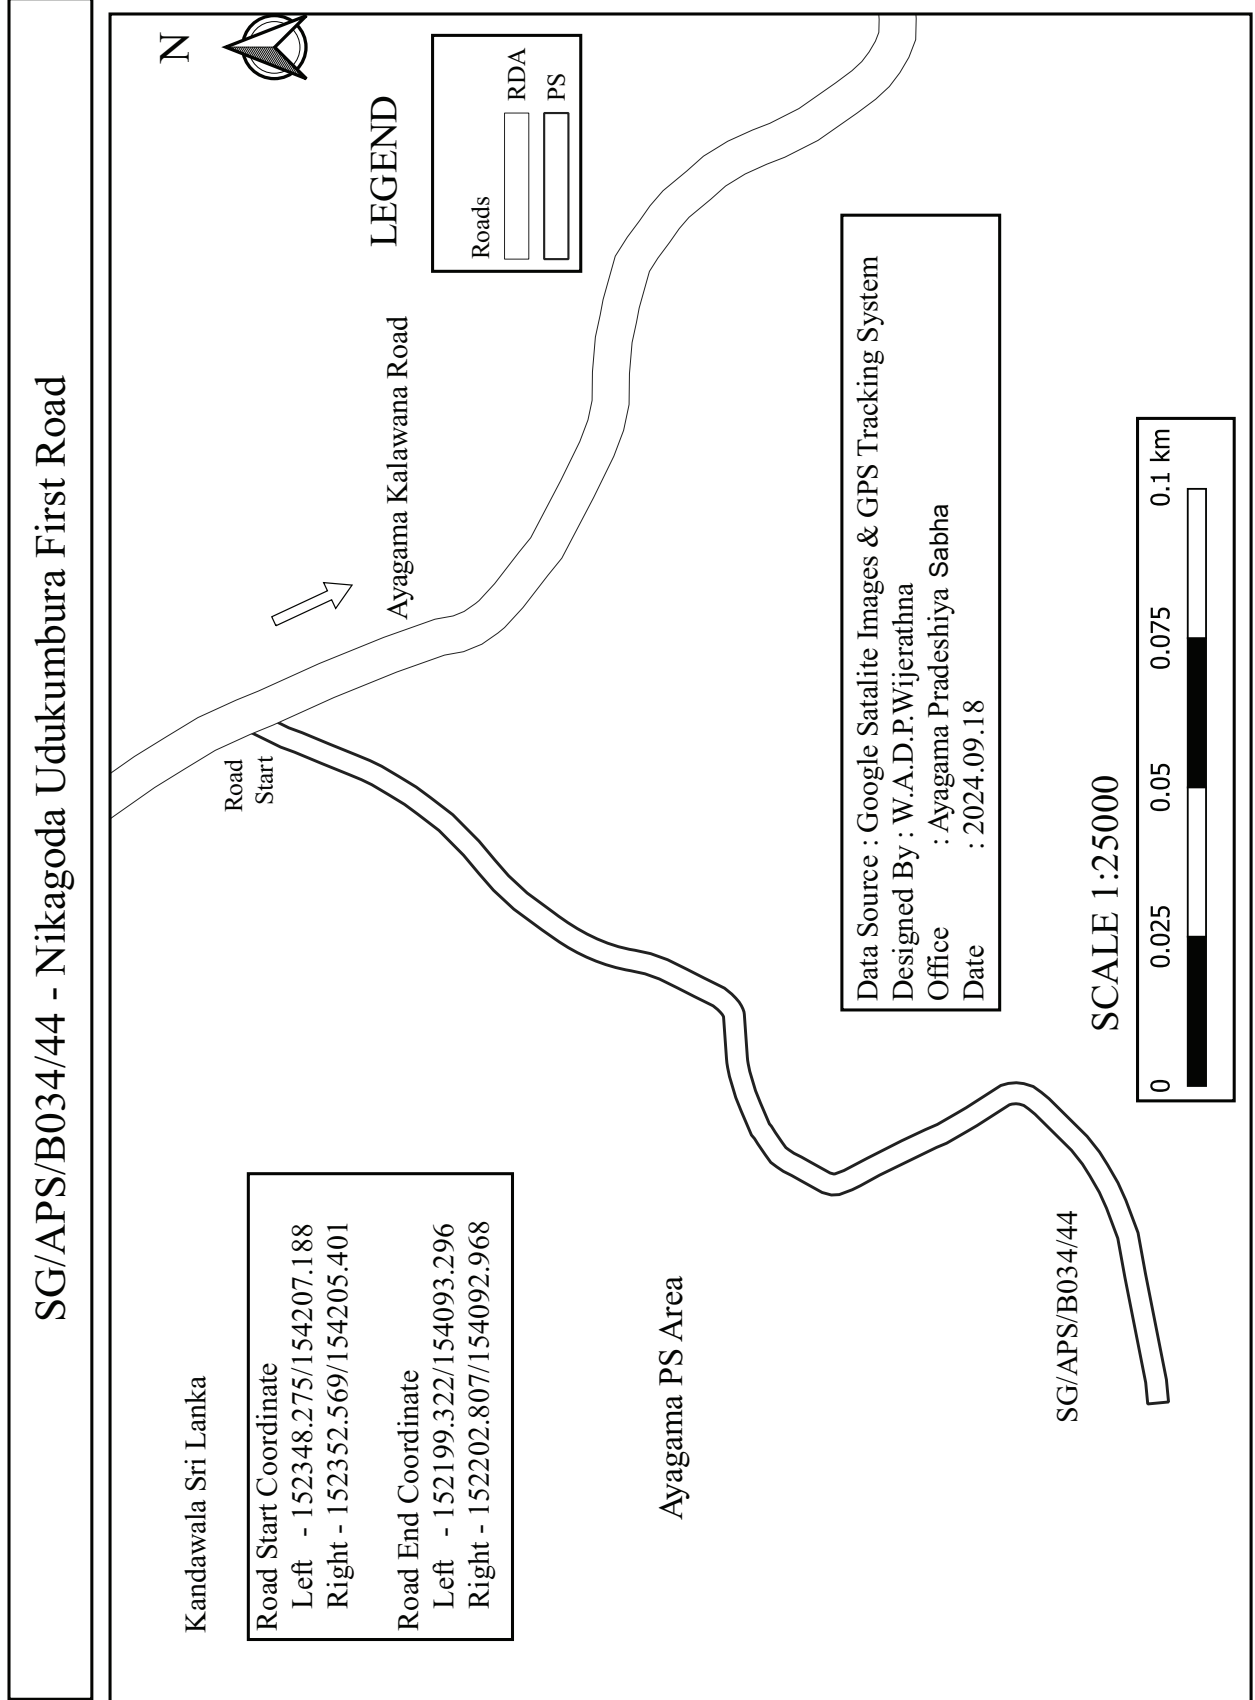


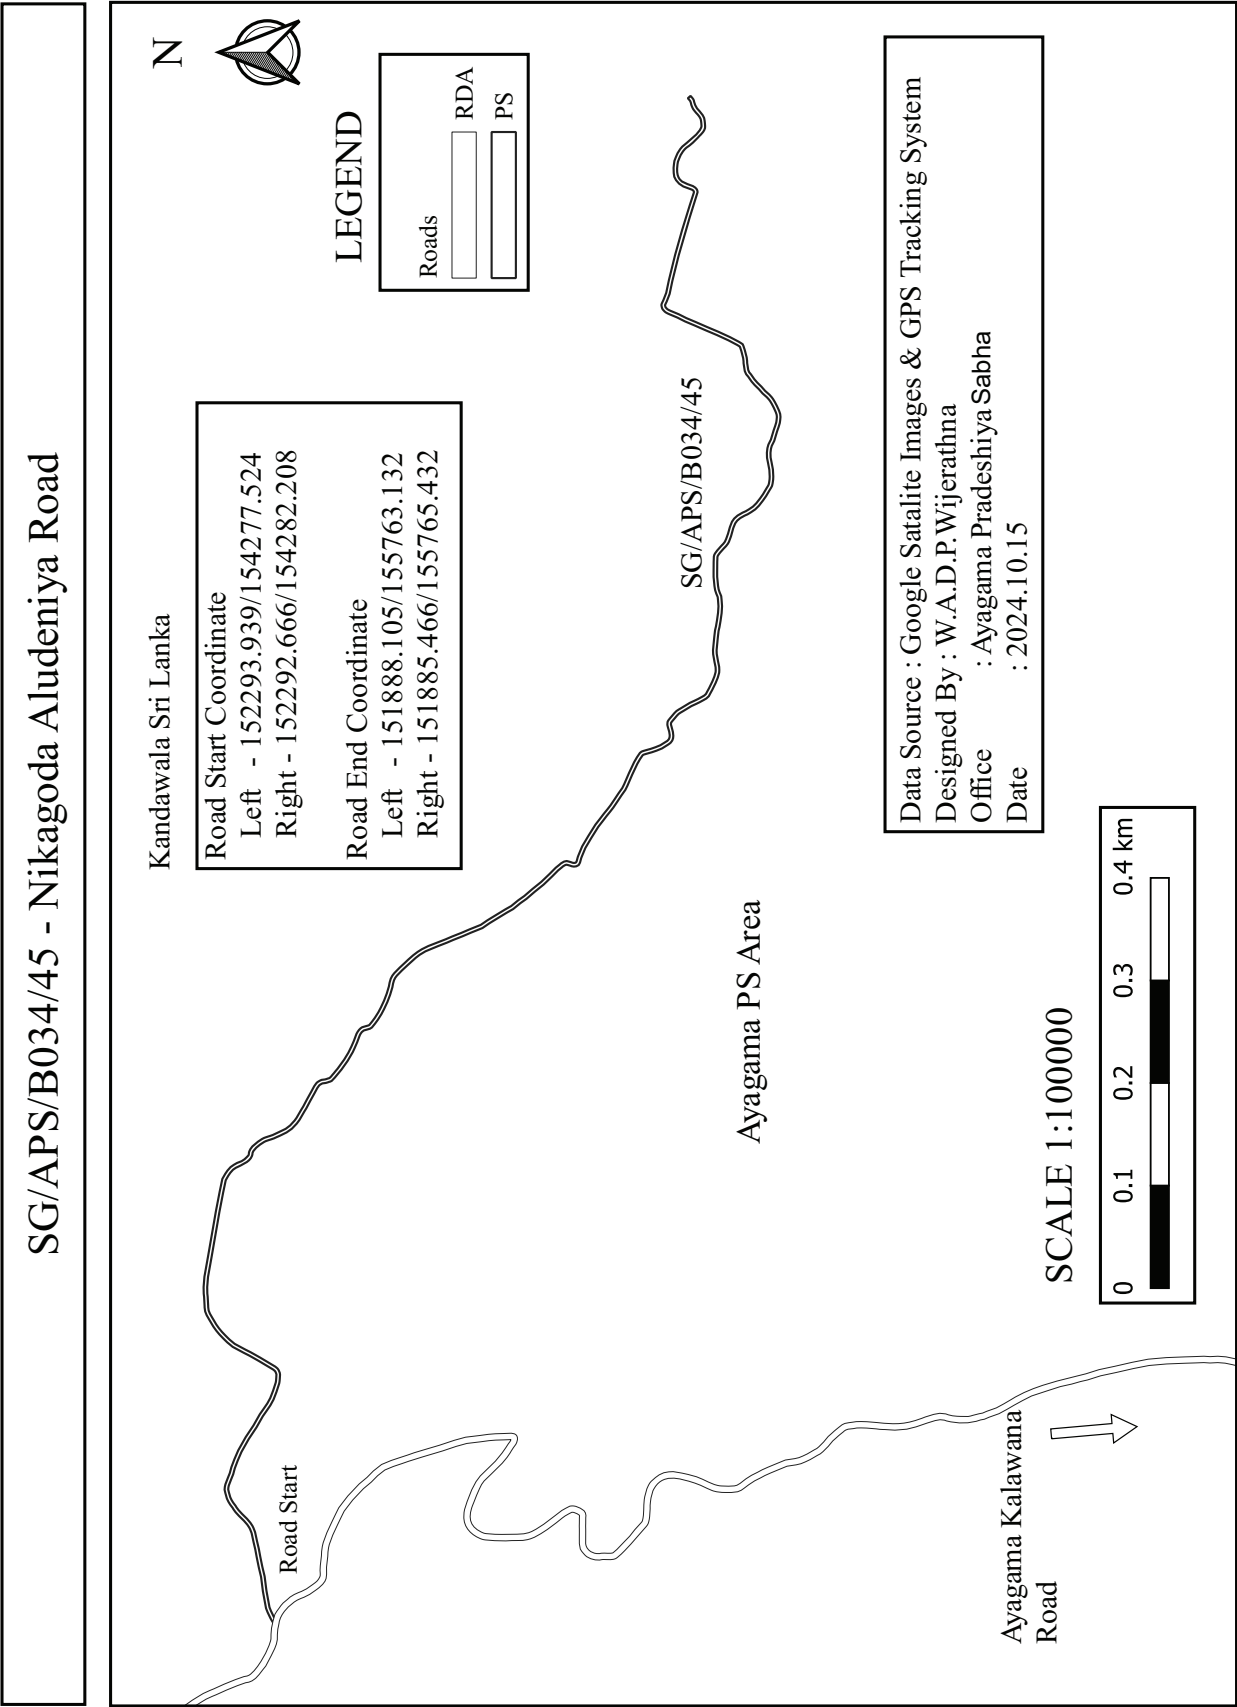

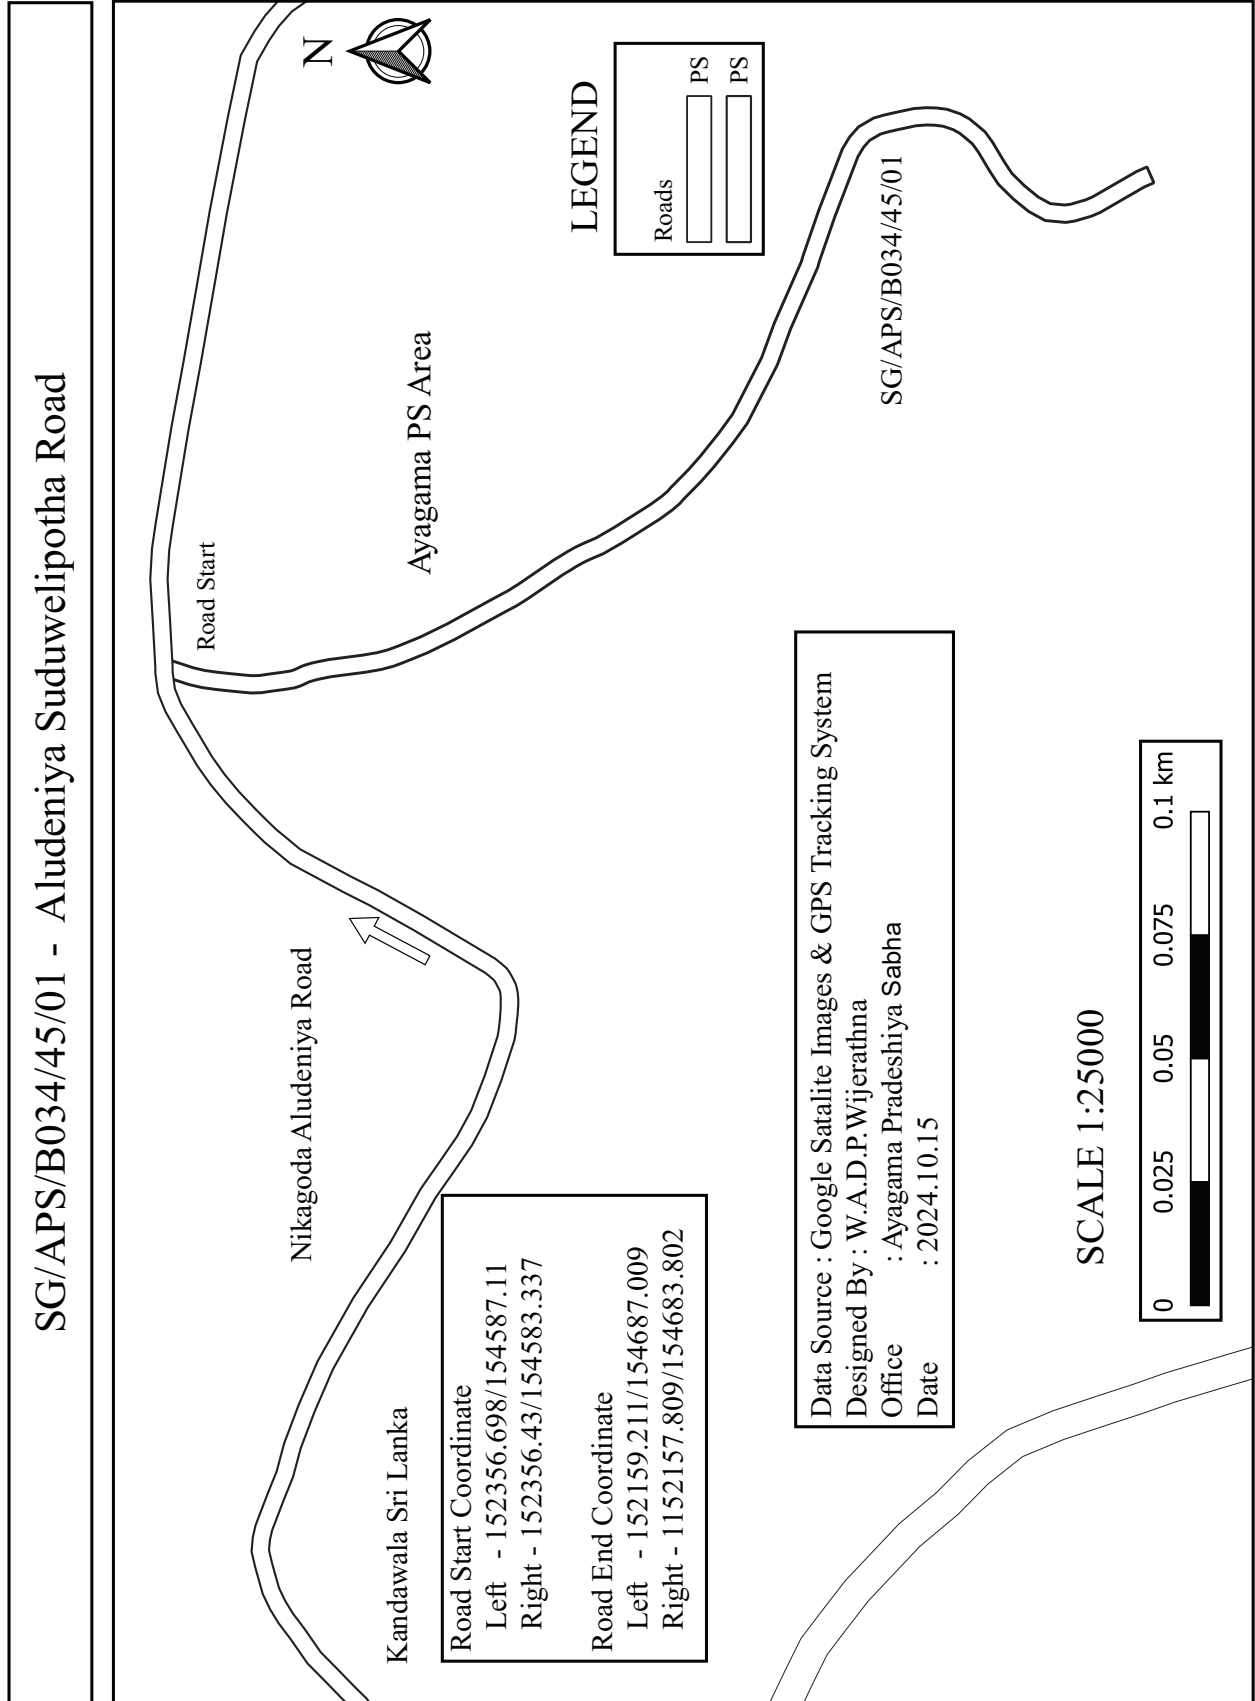

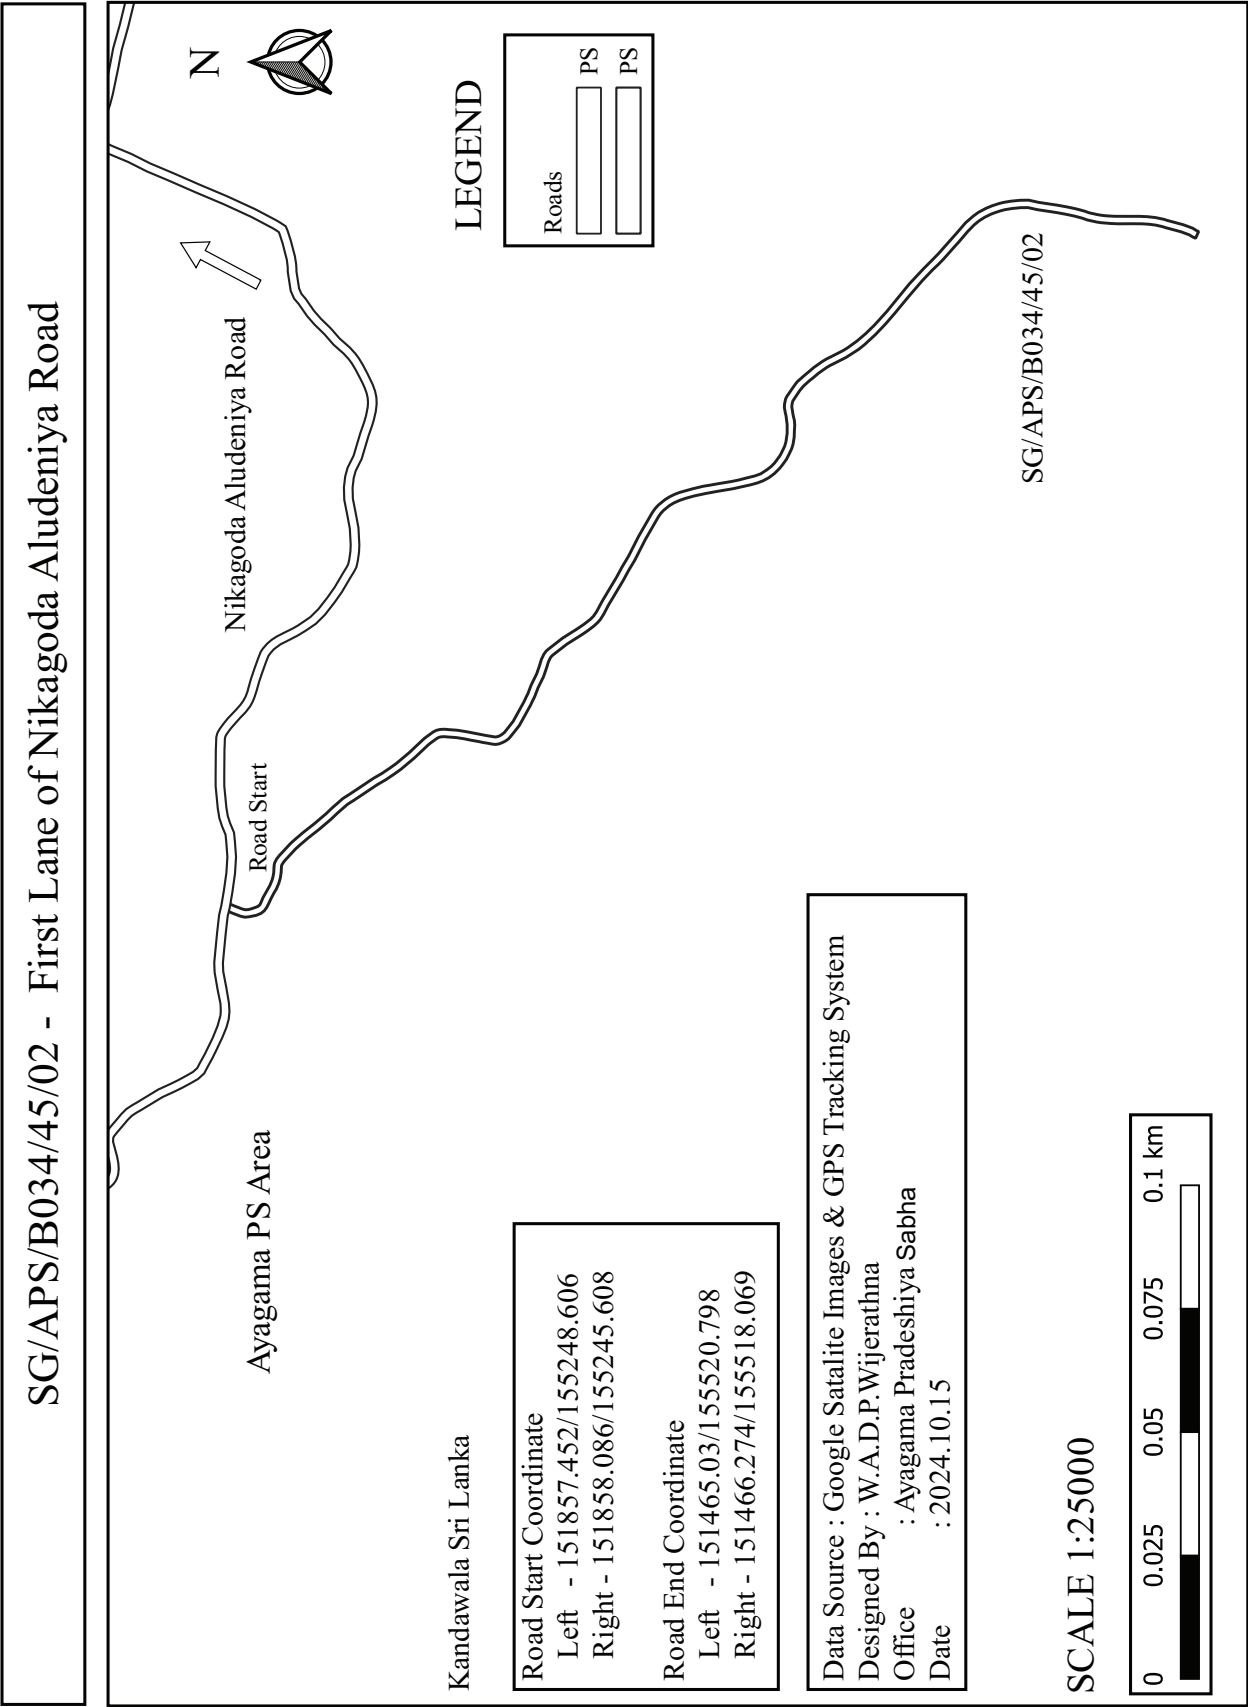

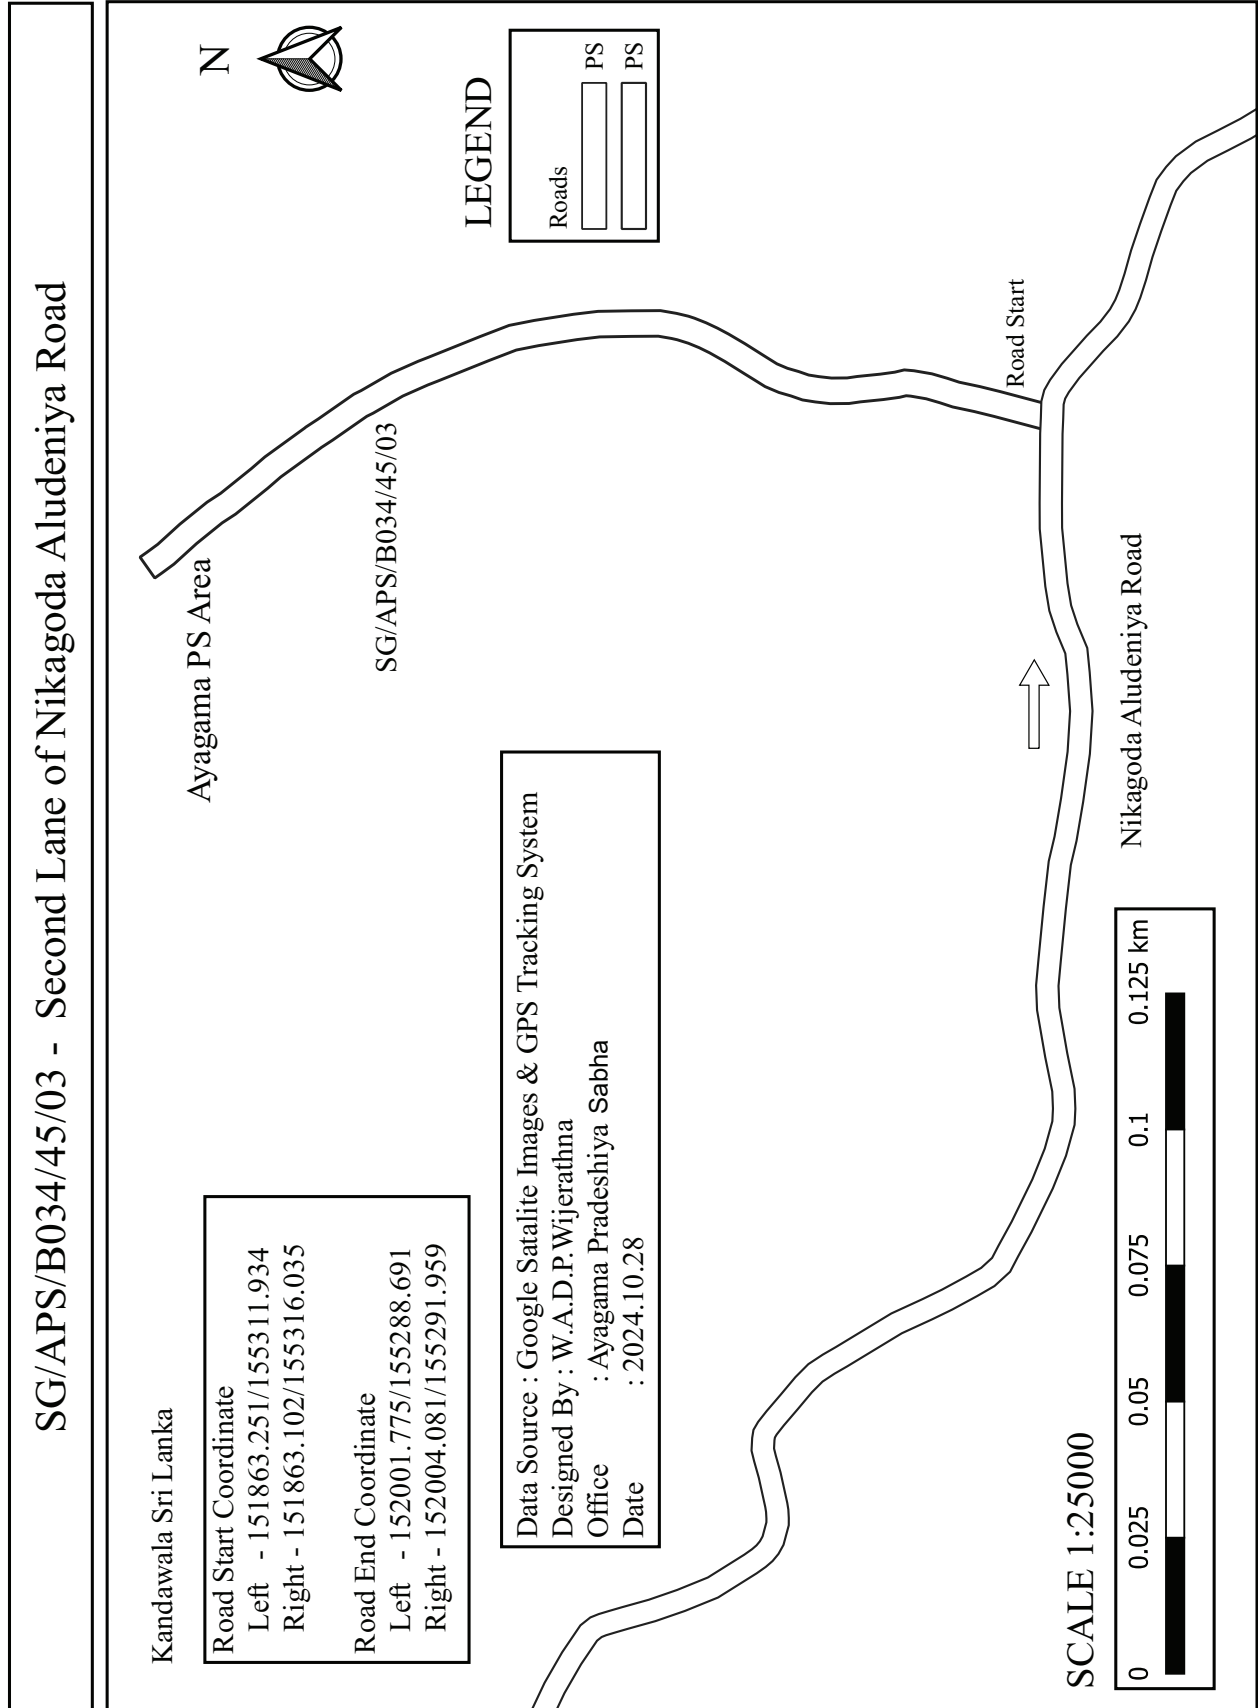

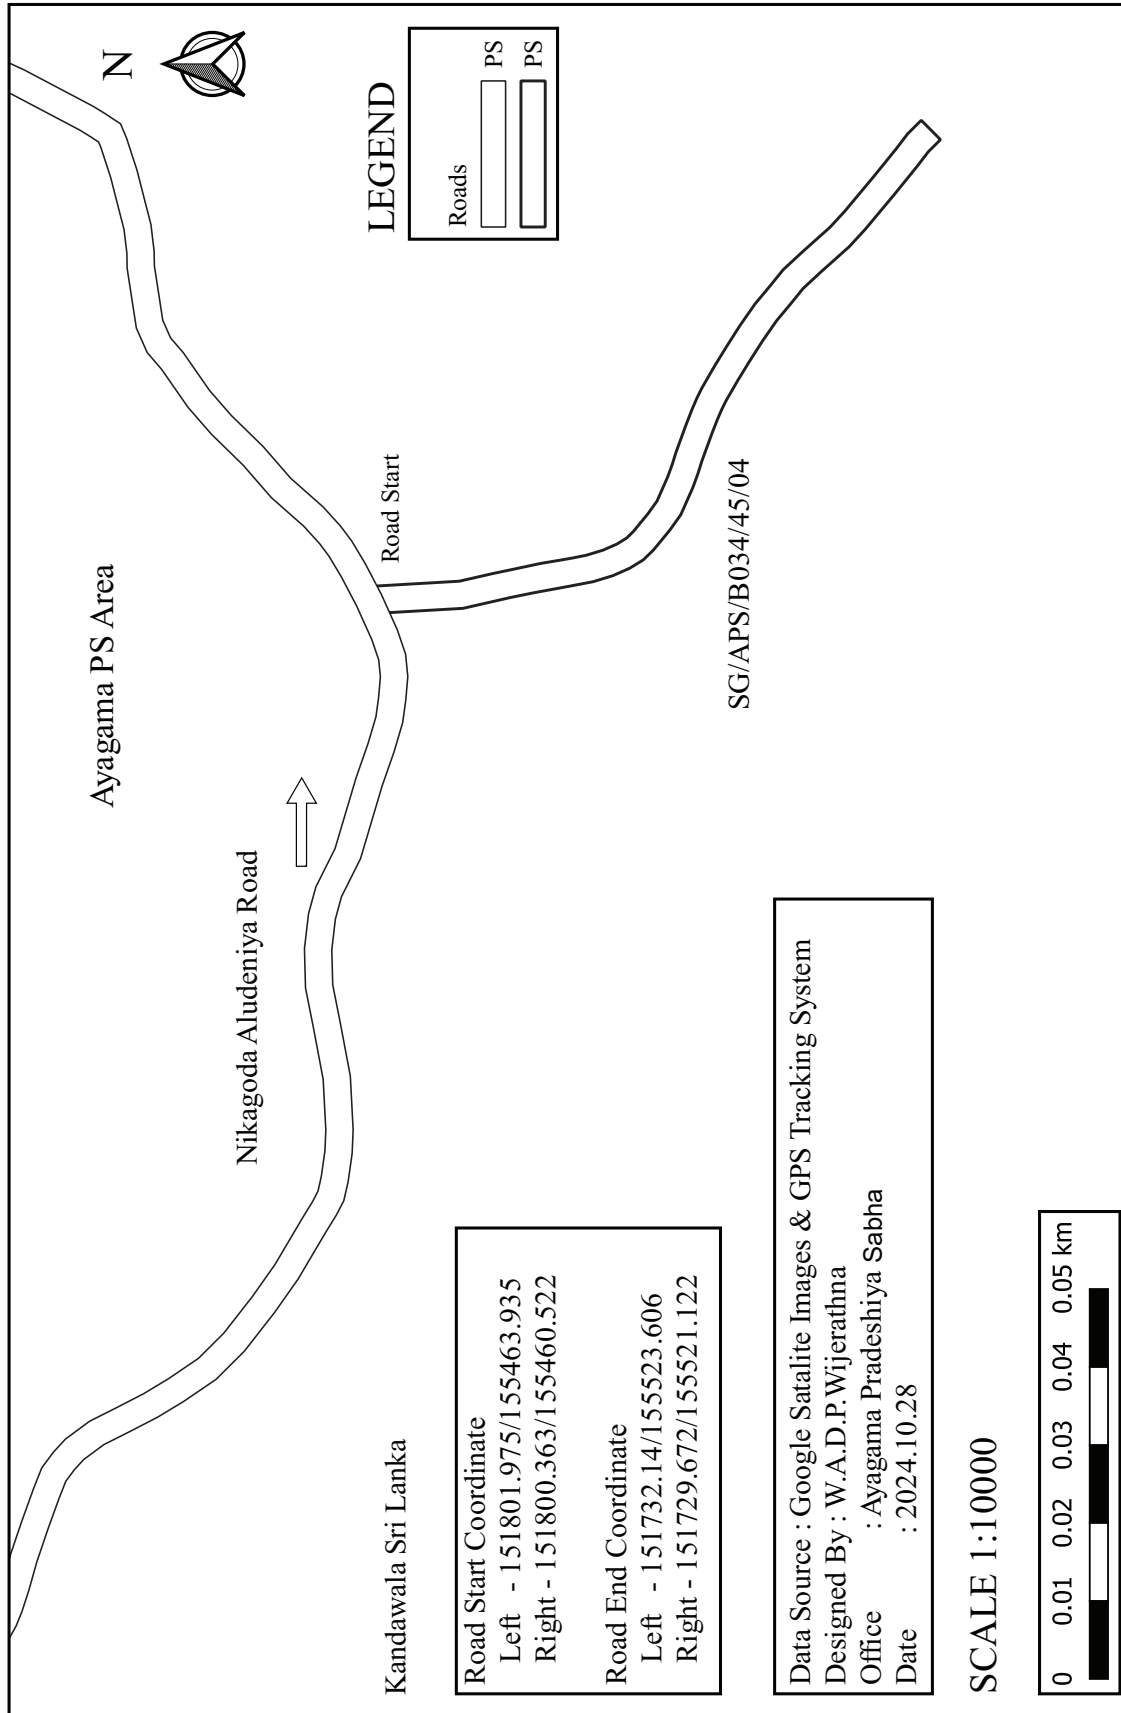

SG/APS/B034/45/05 - Fourth Lane of Nikagoda Aludeniya Road

Kandawala Sri Lanka

Road Start Coordinate

Left - 151836.428/155524.305

Right - 151834.142/155521.646

Road End Coordinate

Left - 151834.407/155586.377

Right - 151835.461/155589.714


Data Source : Google Satalite Images & GPS Tracking System

Designed By : W.A.D.P.Wijerathna

Office : Ayagama Pradeshiya Sabha

Date : 2024.10.28

SCALE 1:10000

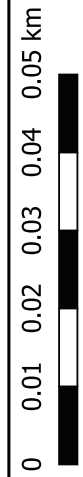

Ayagama PS Area



LEGEND


Roads




Road Start


Nikagoda Aludeniya Road


SG/APS/B034/45/05

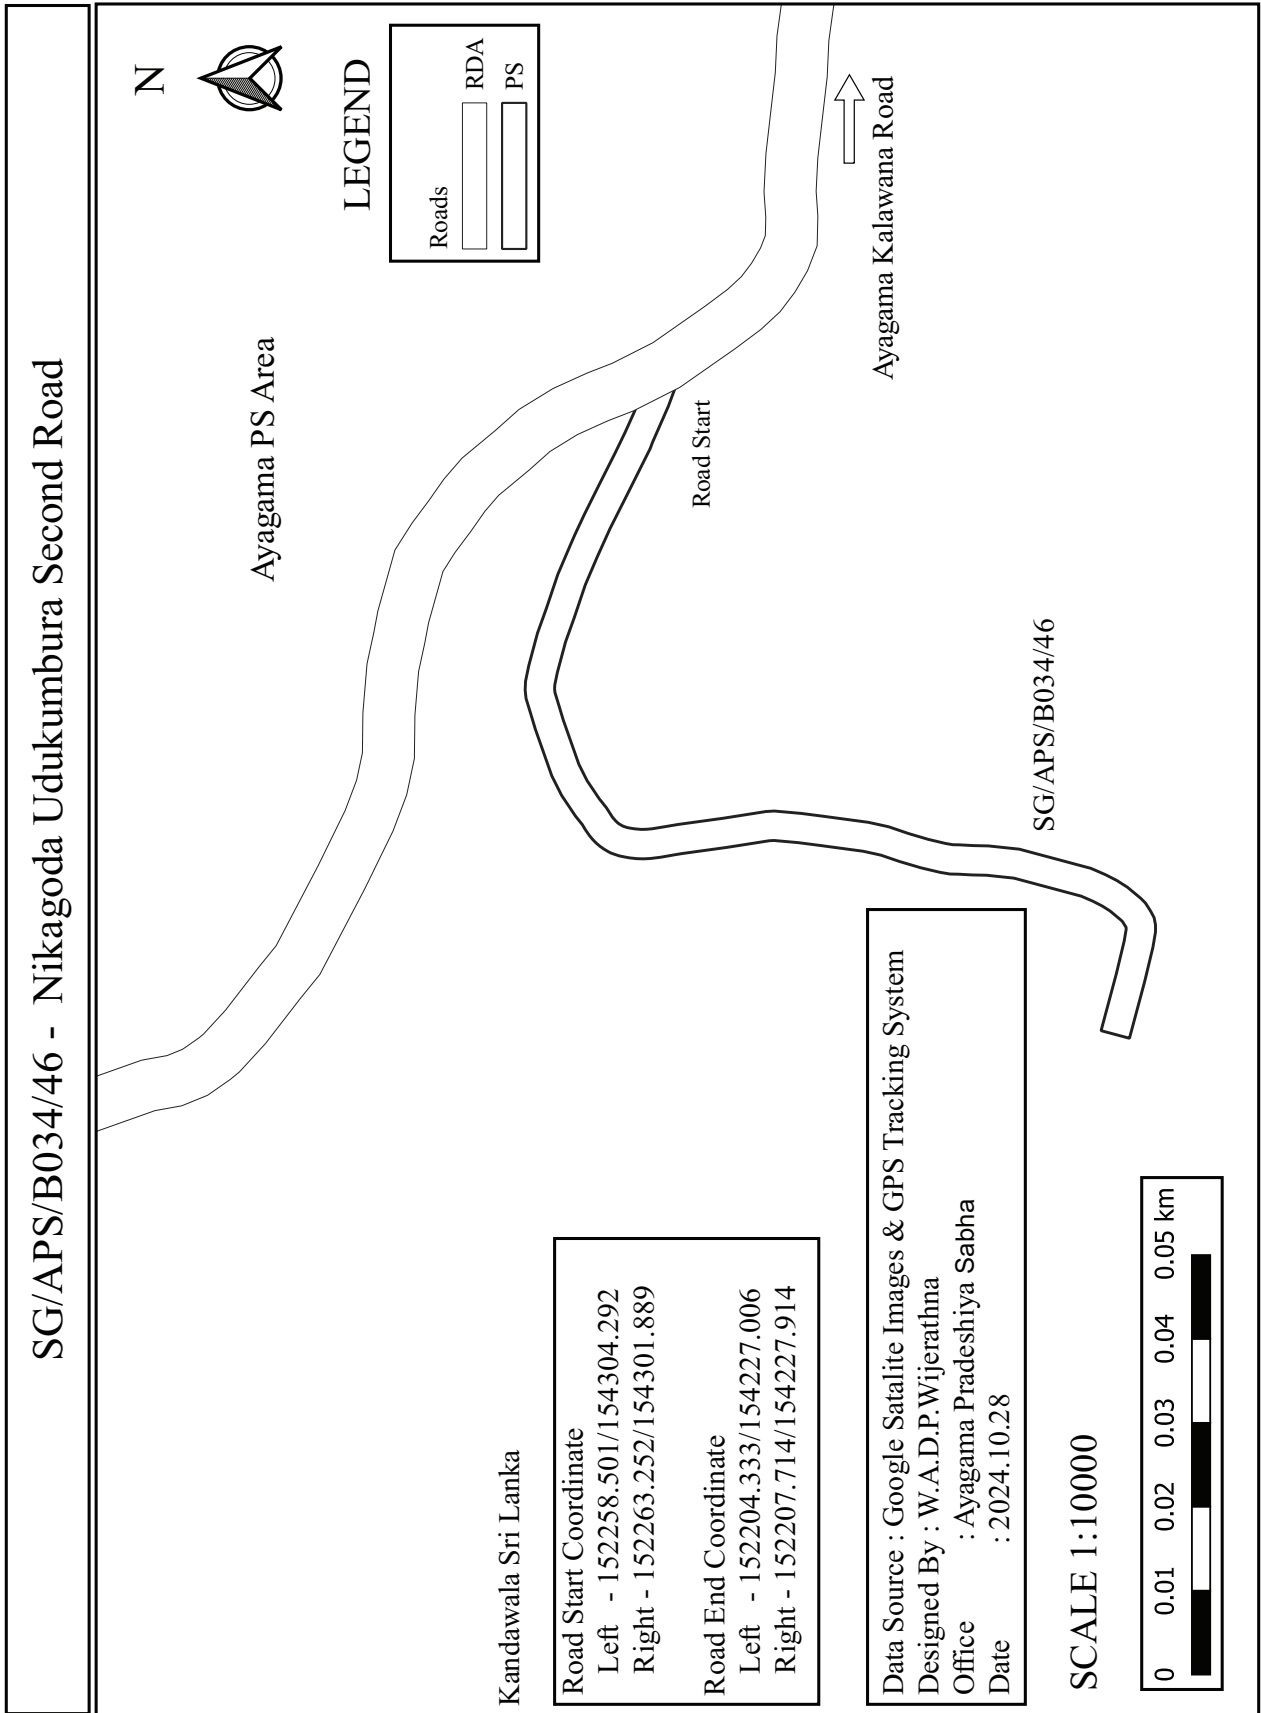

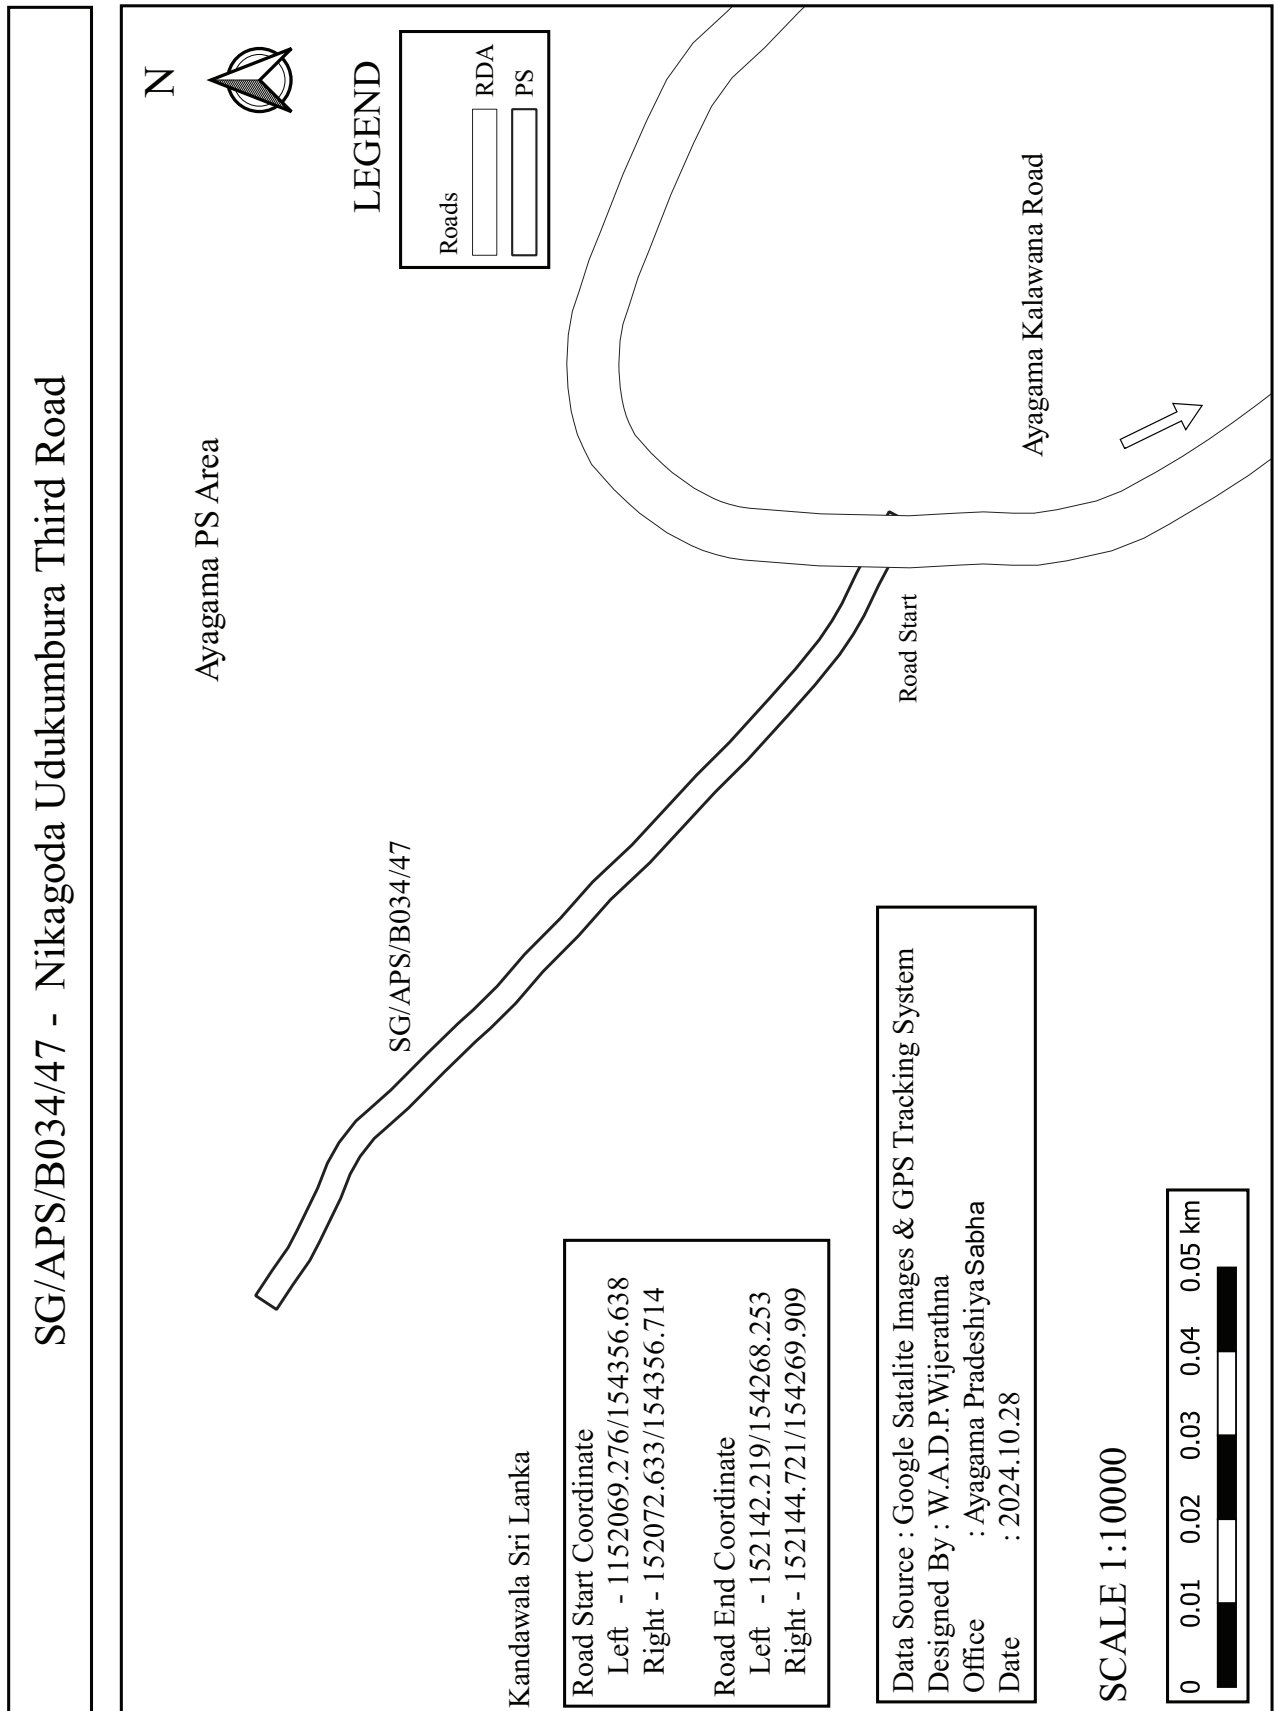


SG/APS/B034/48 - First Lane of Nikagoda

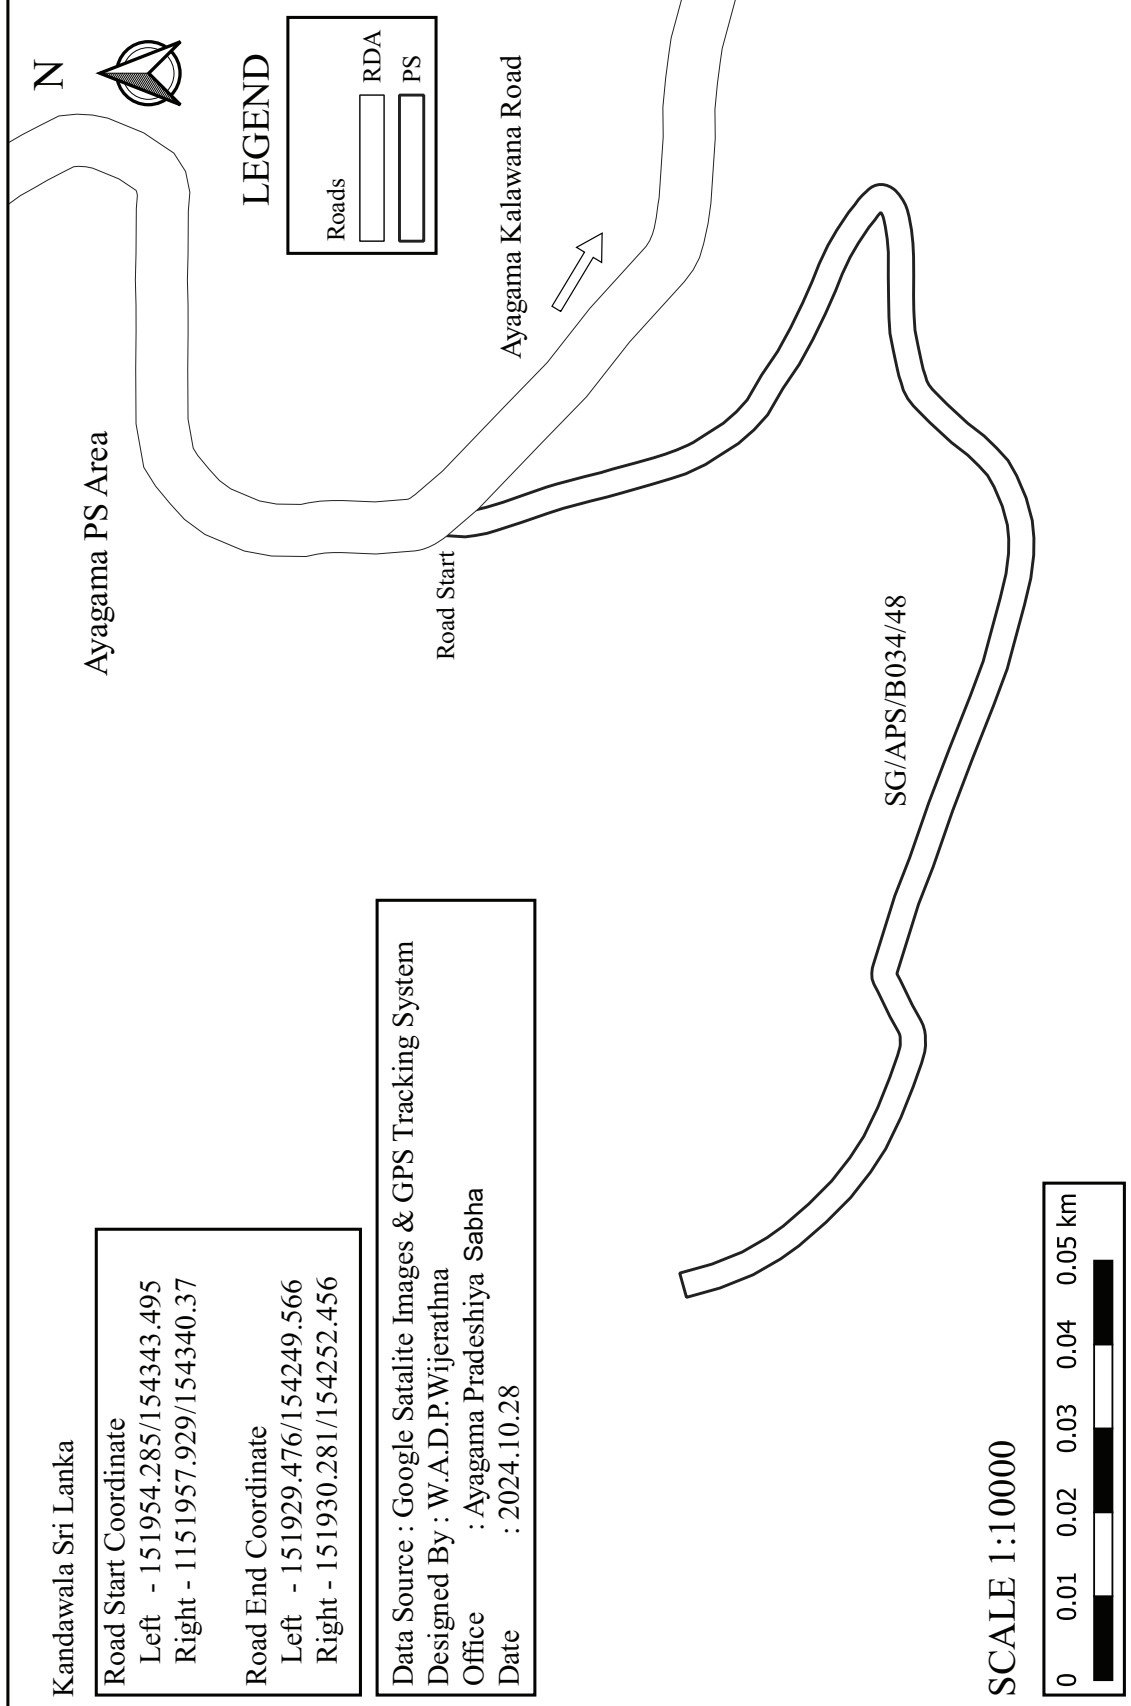

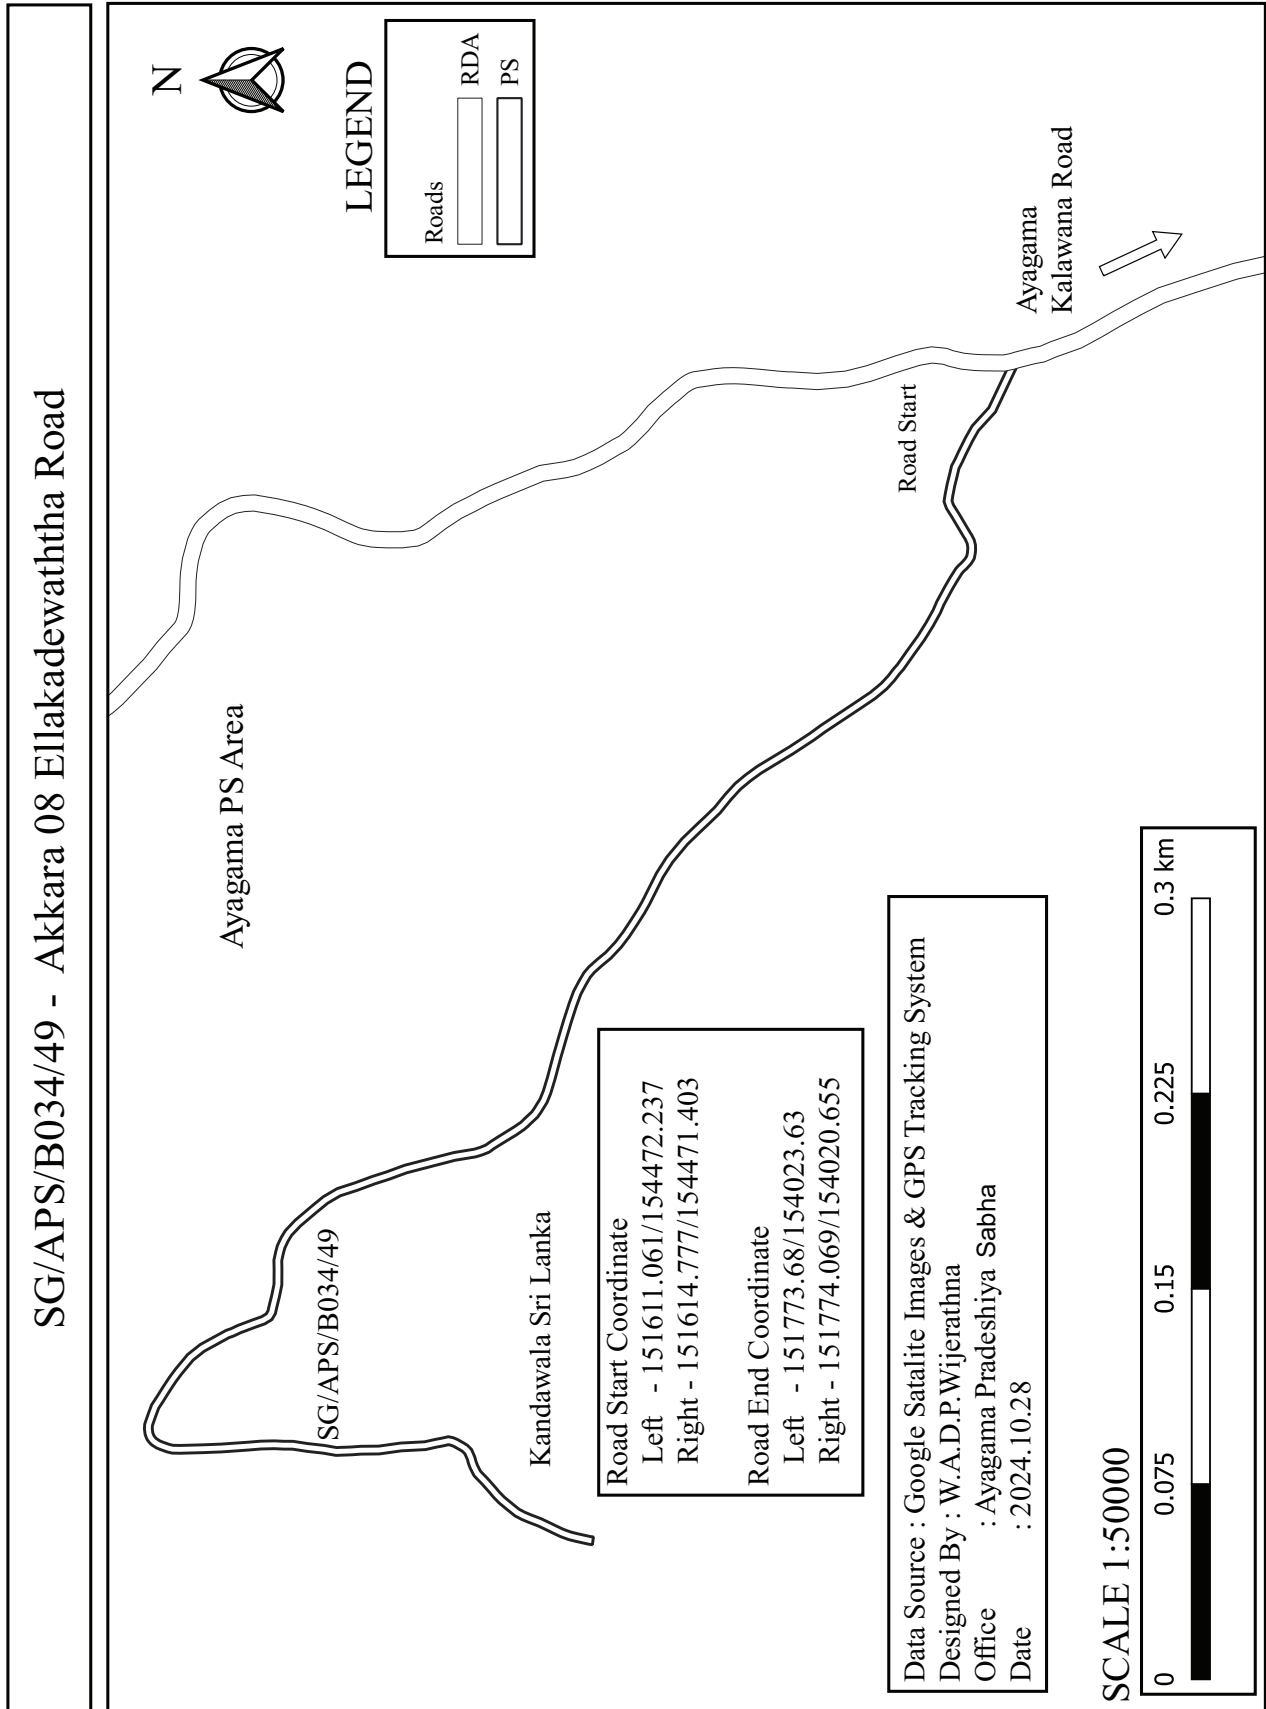


SG/APS/B034/49/01 - Akkara 05 Imbulahithihena Road

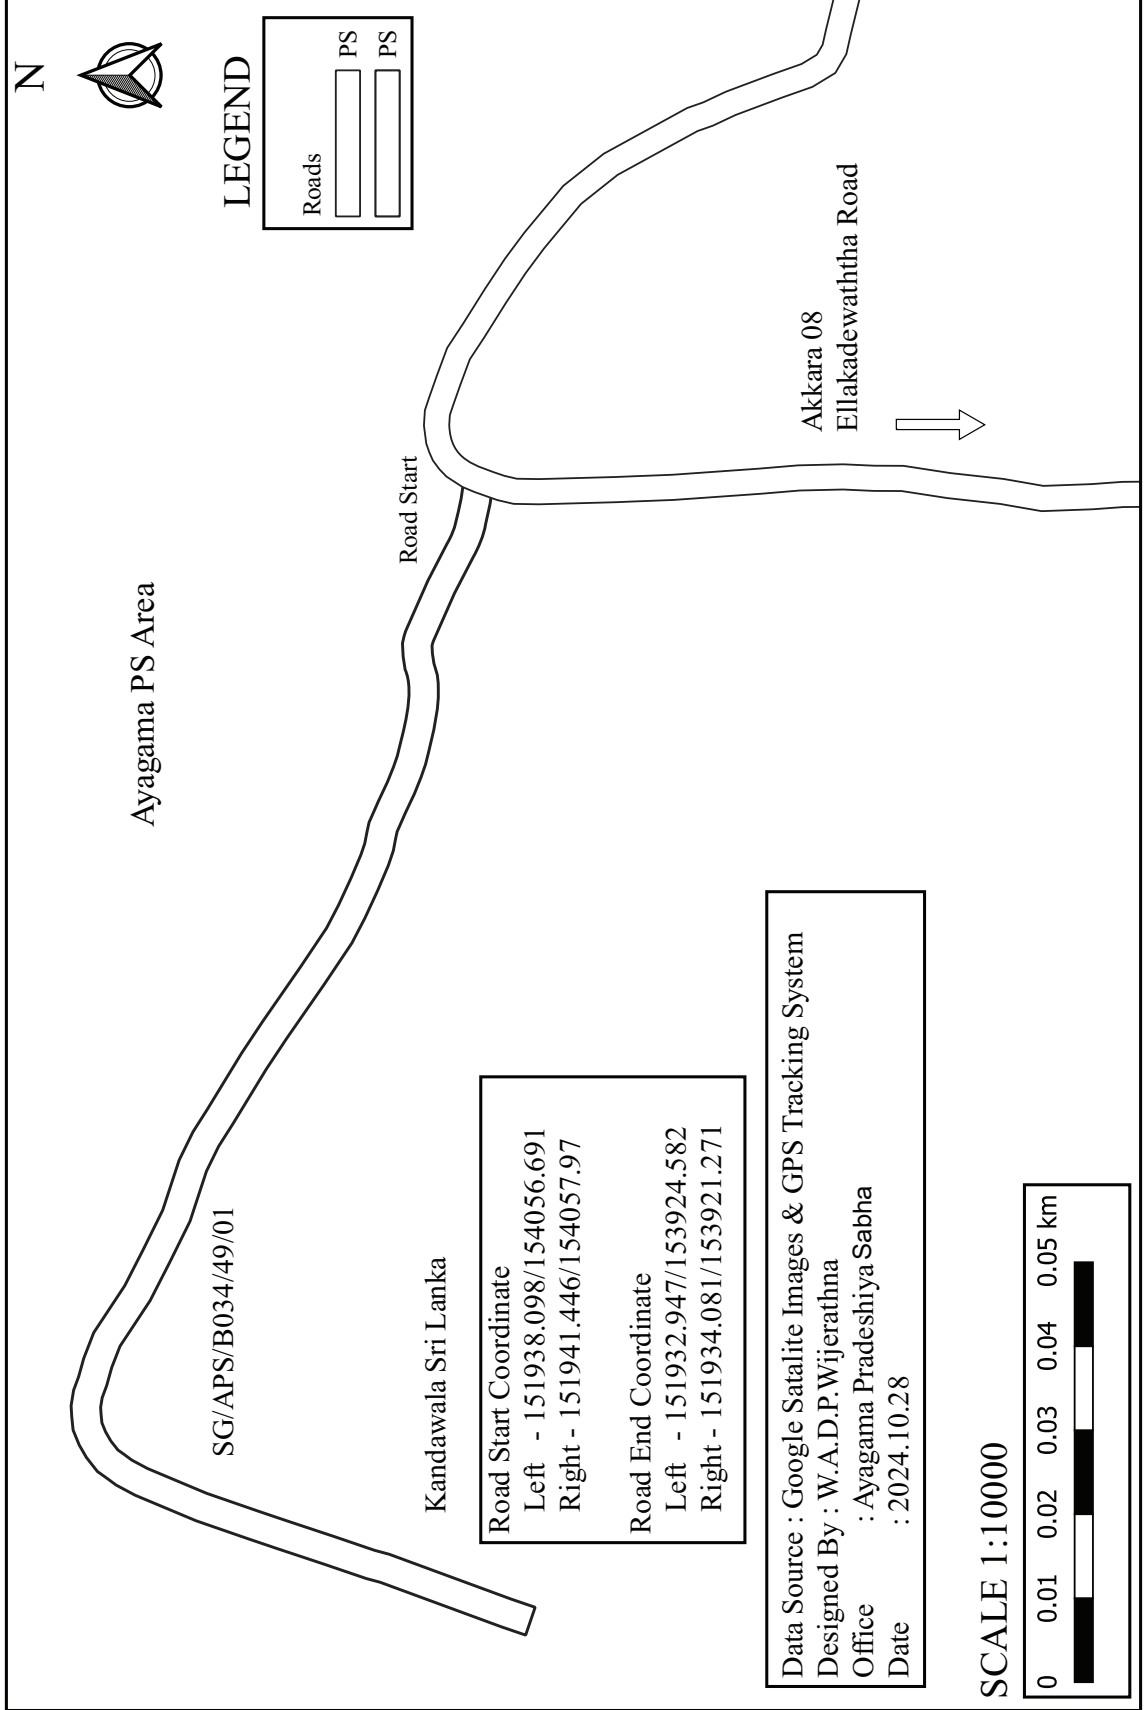



IV(අ) : කොටස - ශ්‍රී ලංකා ප්‍රජාතාන්ත්‍රික සමාජවාදී ජනරජයේ අති විශේෂ ගැසට් පත්‍රය - 2026.01.01


191A


ප්‍රති IV(ආ) - இலங்கைச் சனநாயக சோசலிசக் குடியரசு வர்த்தமானப் பத்திரிகை - அதி விசேஷமானது - 2026.01.01

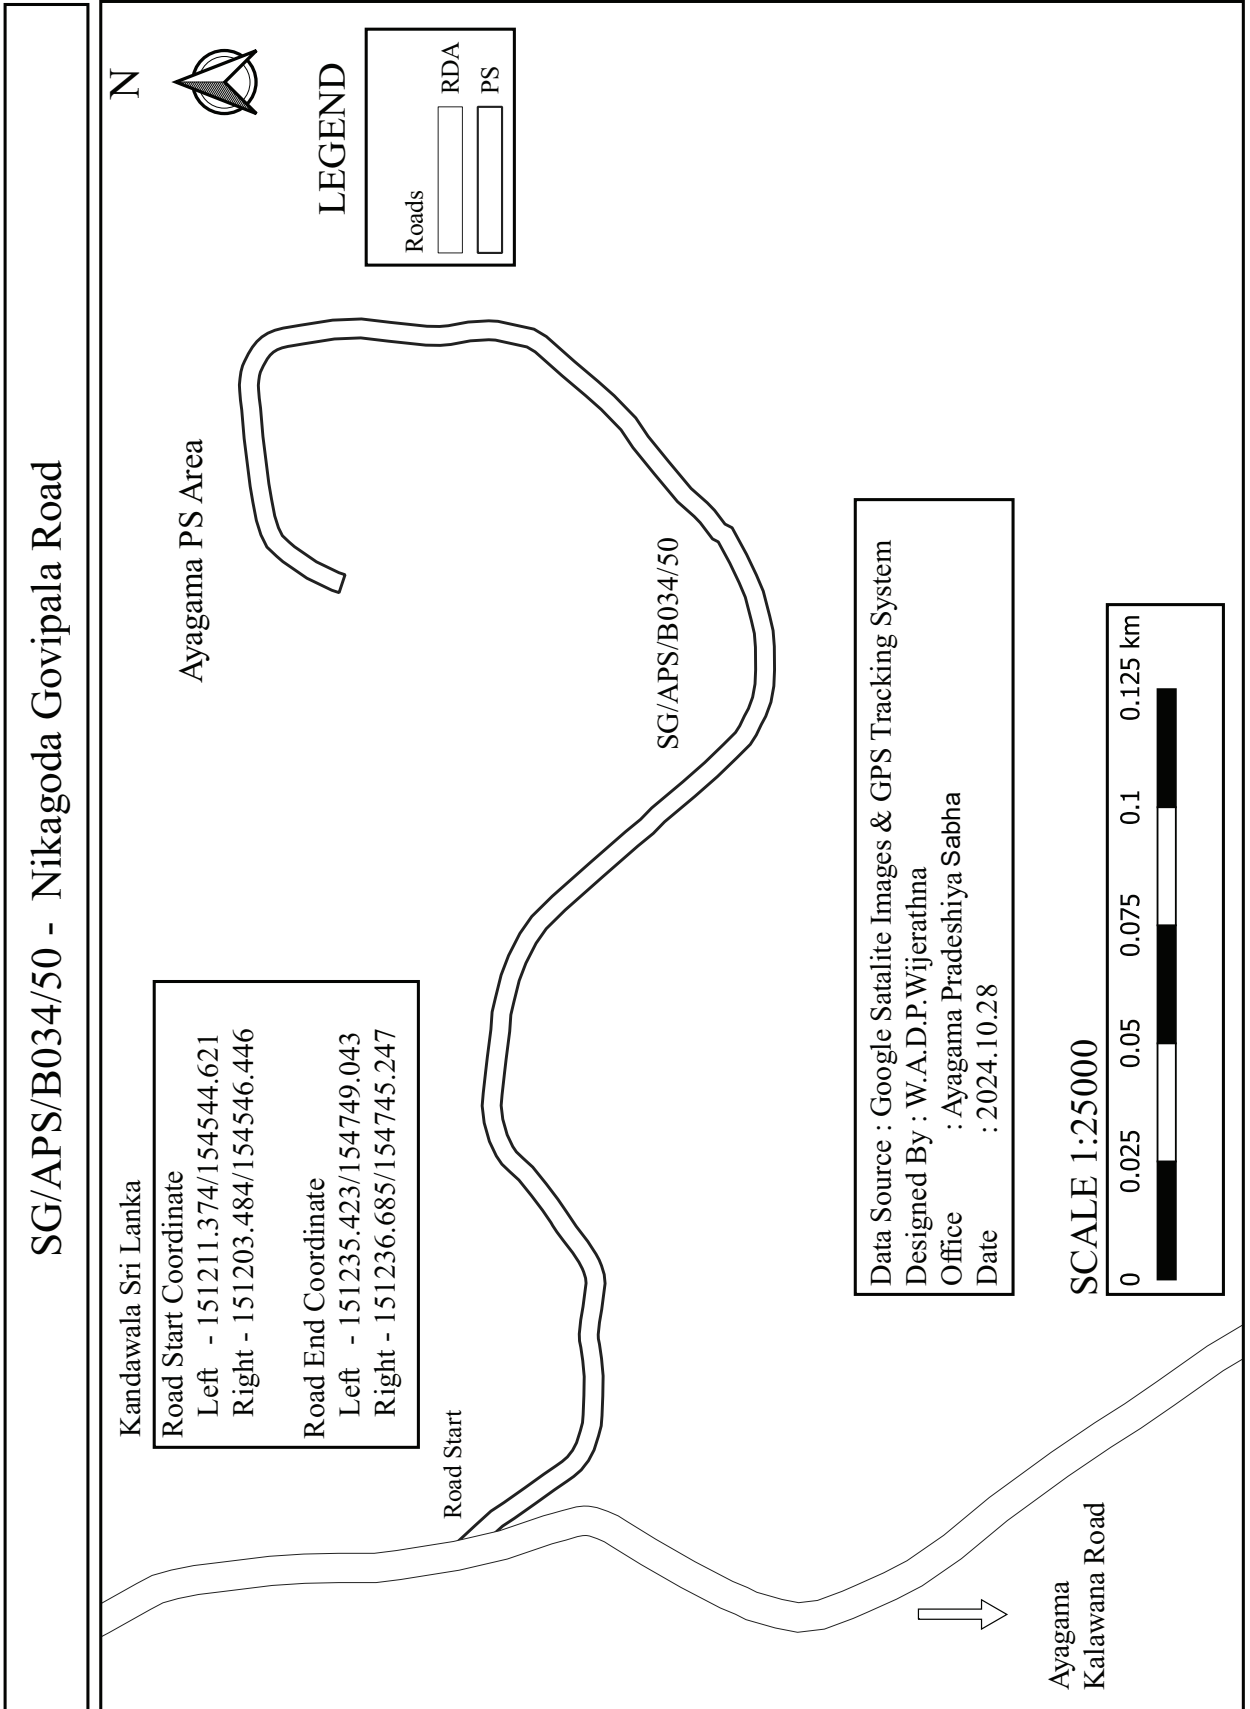


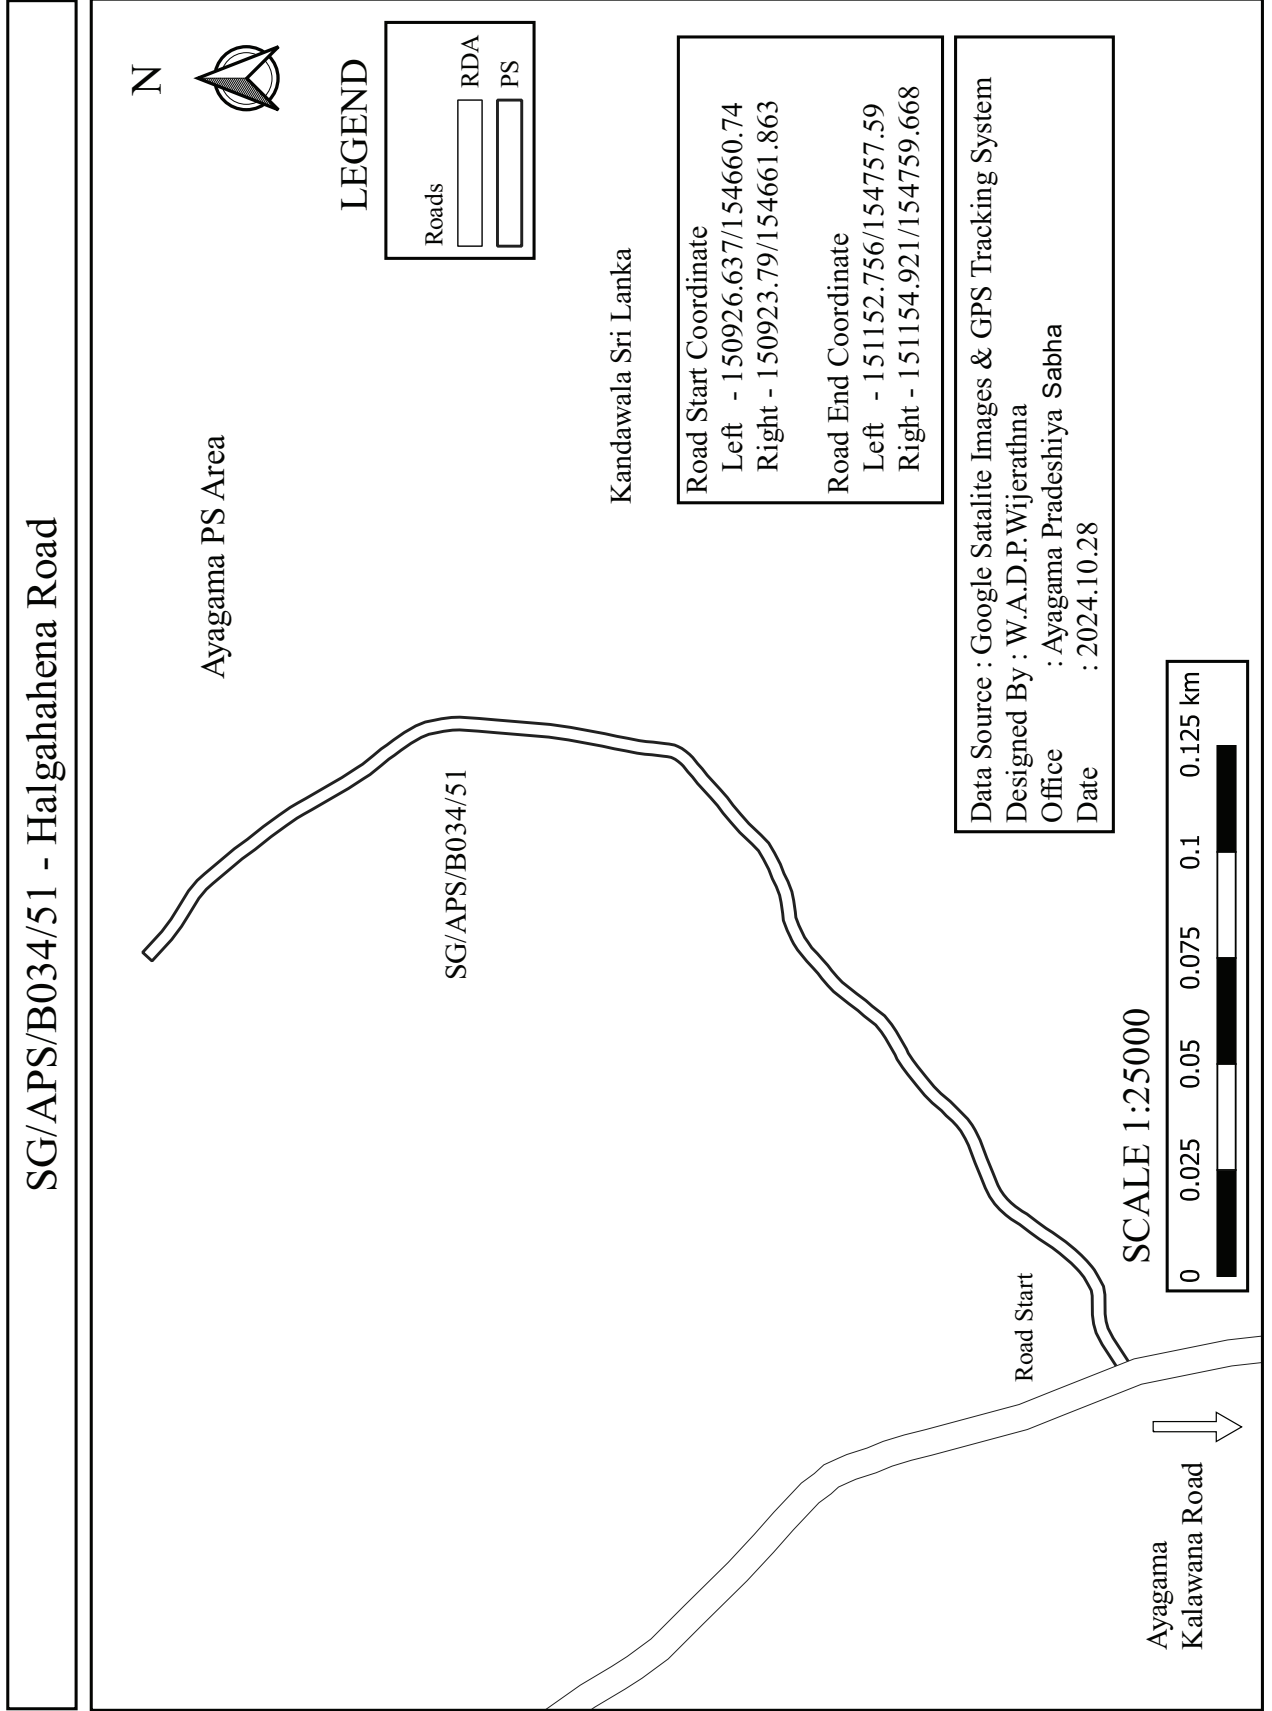


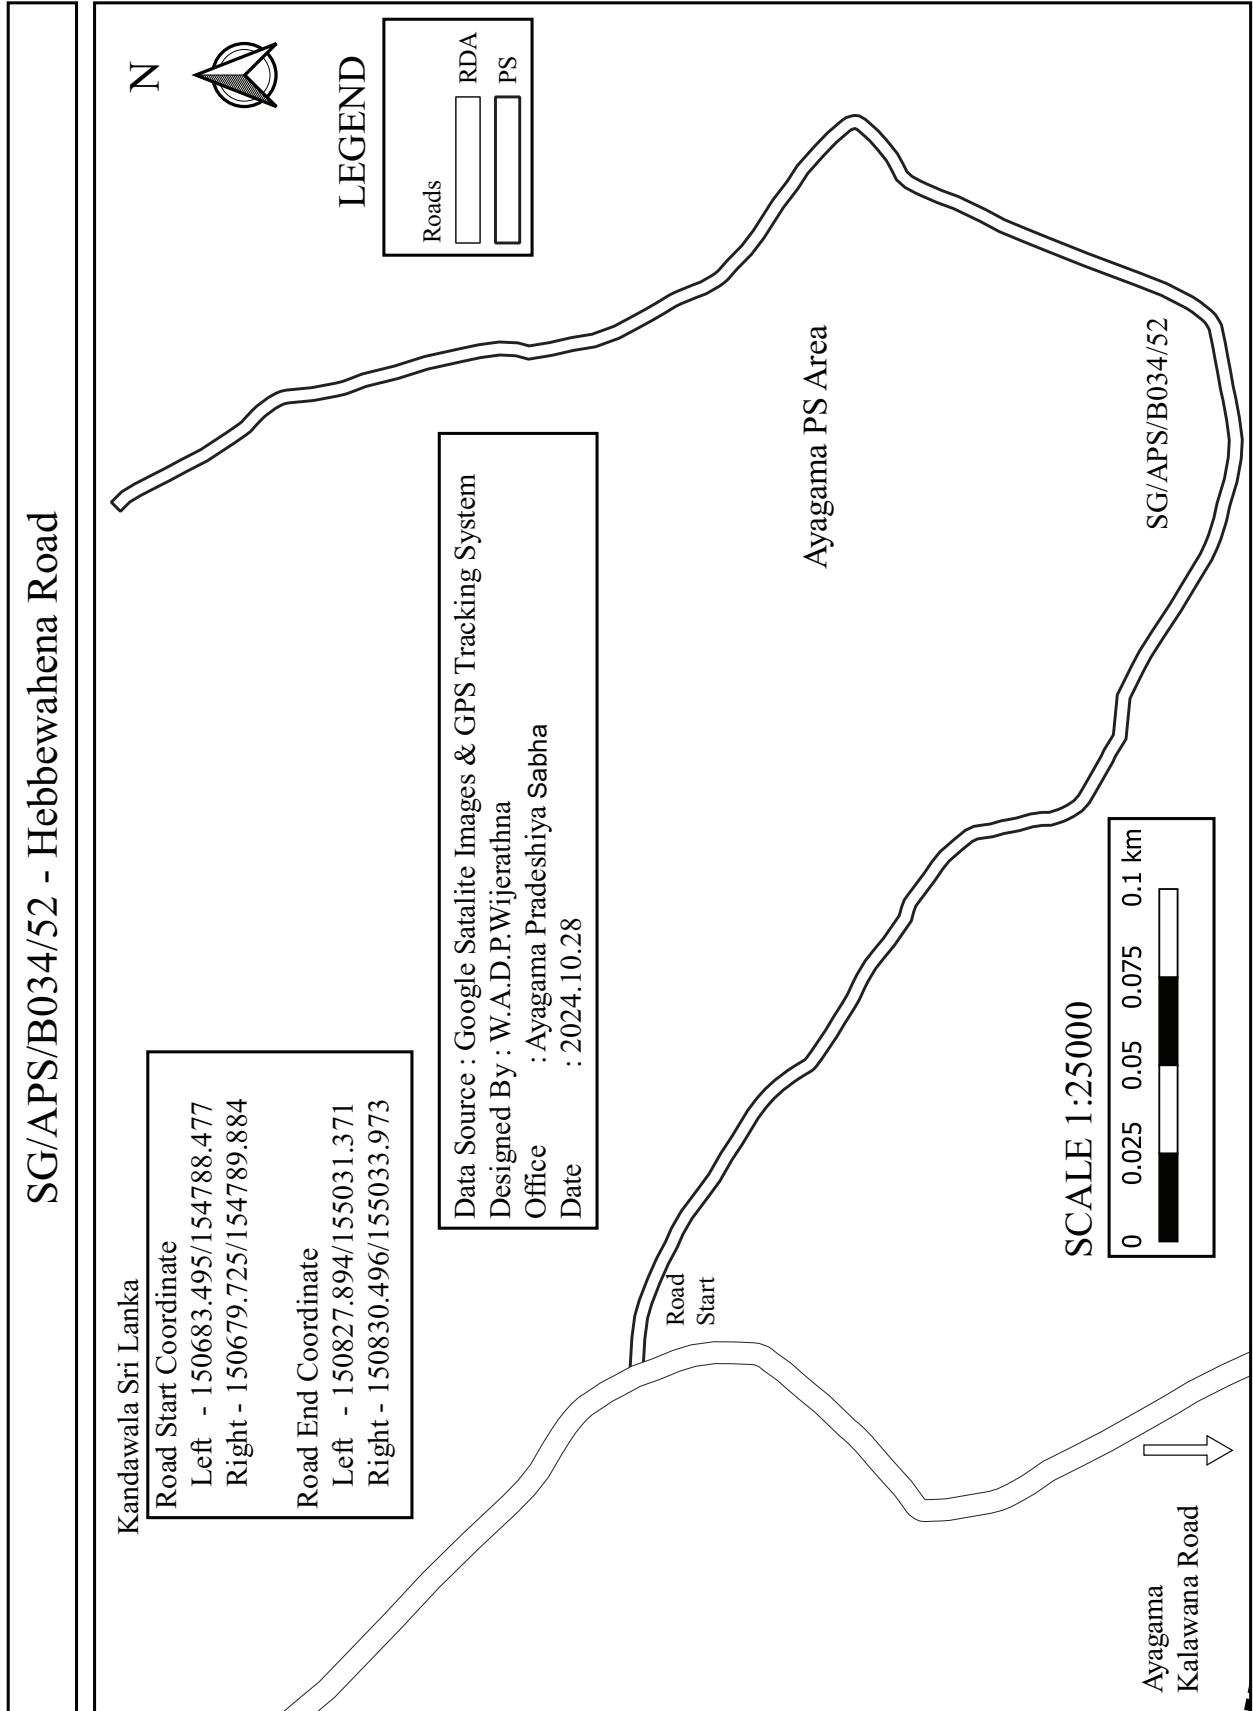


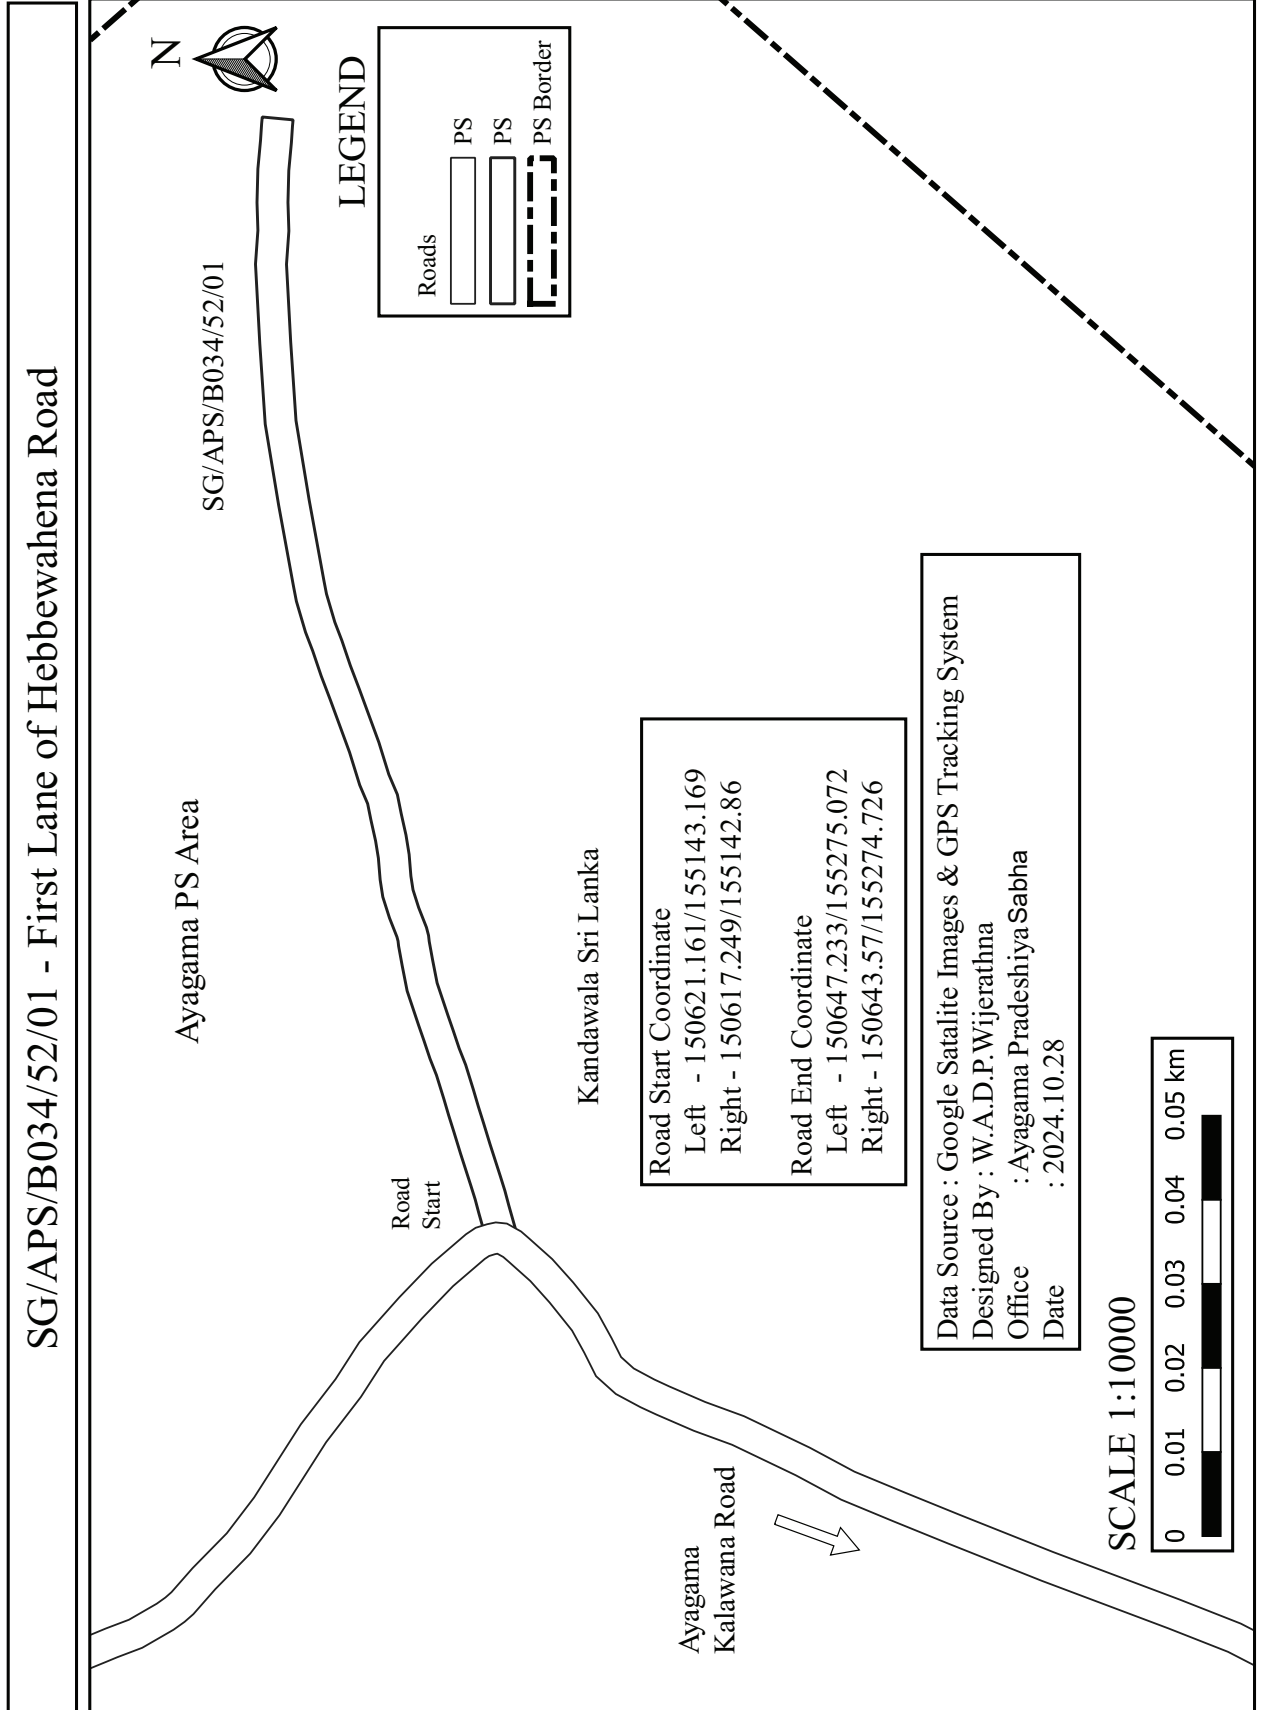


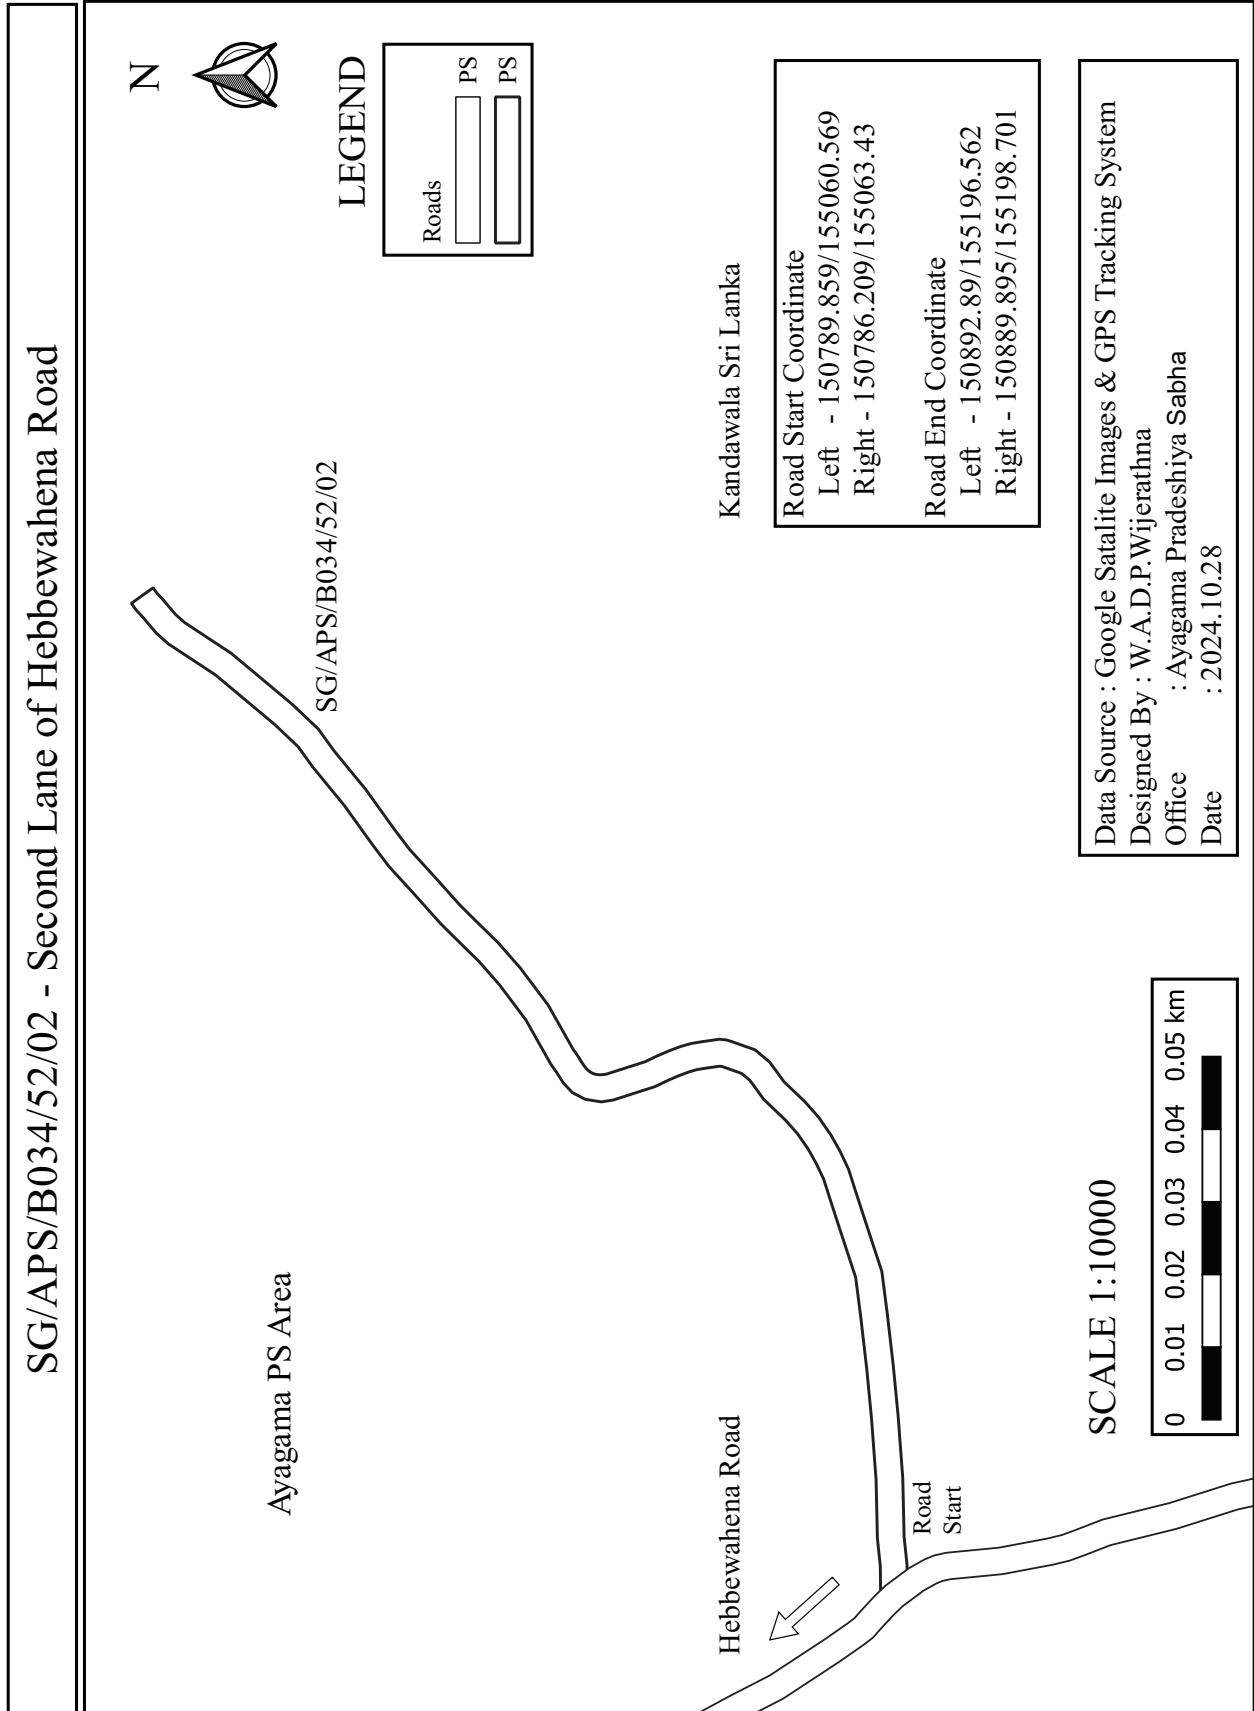


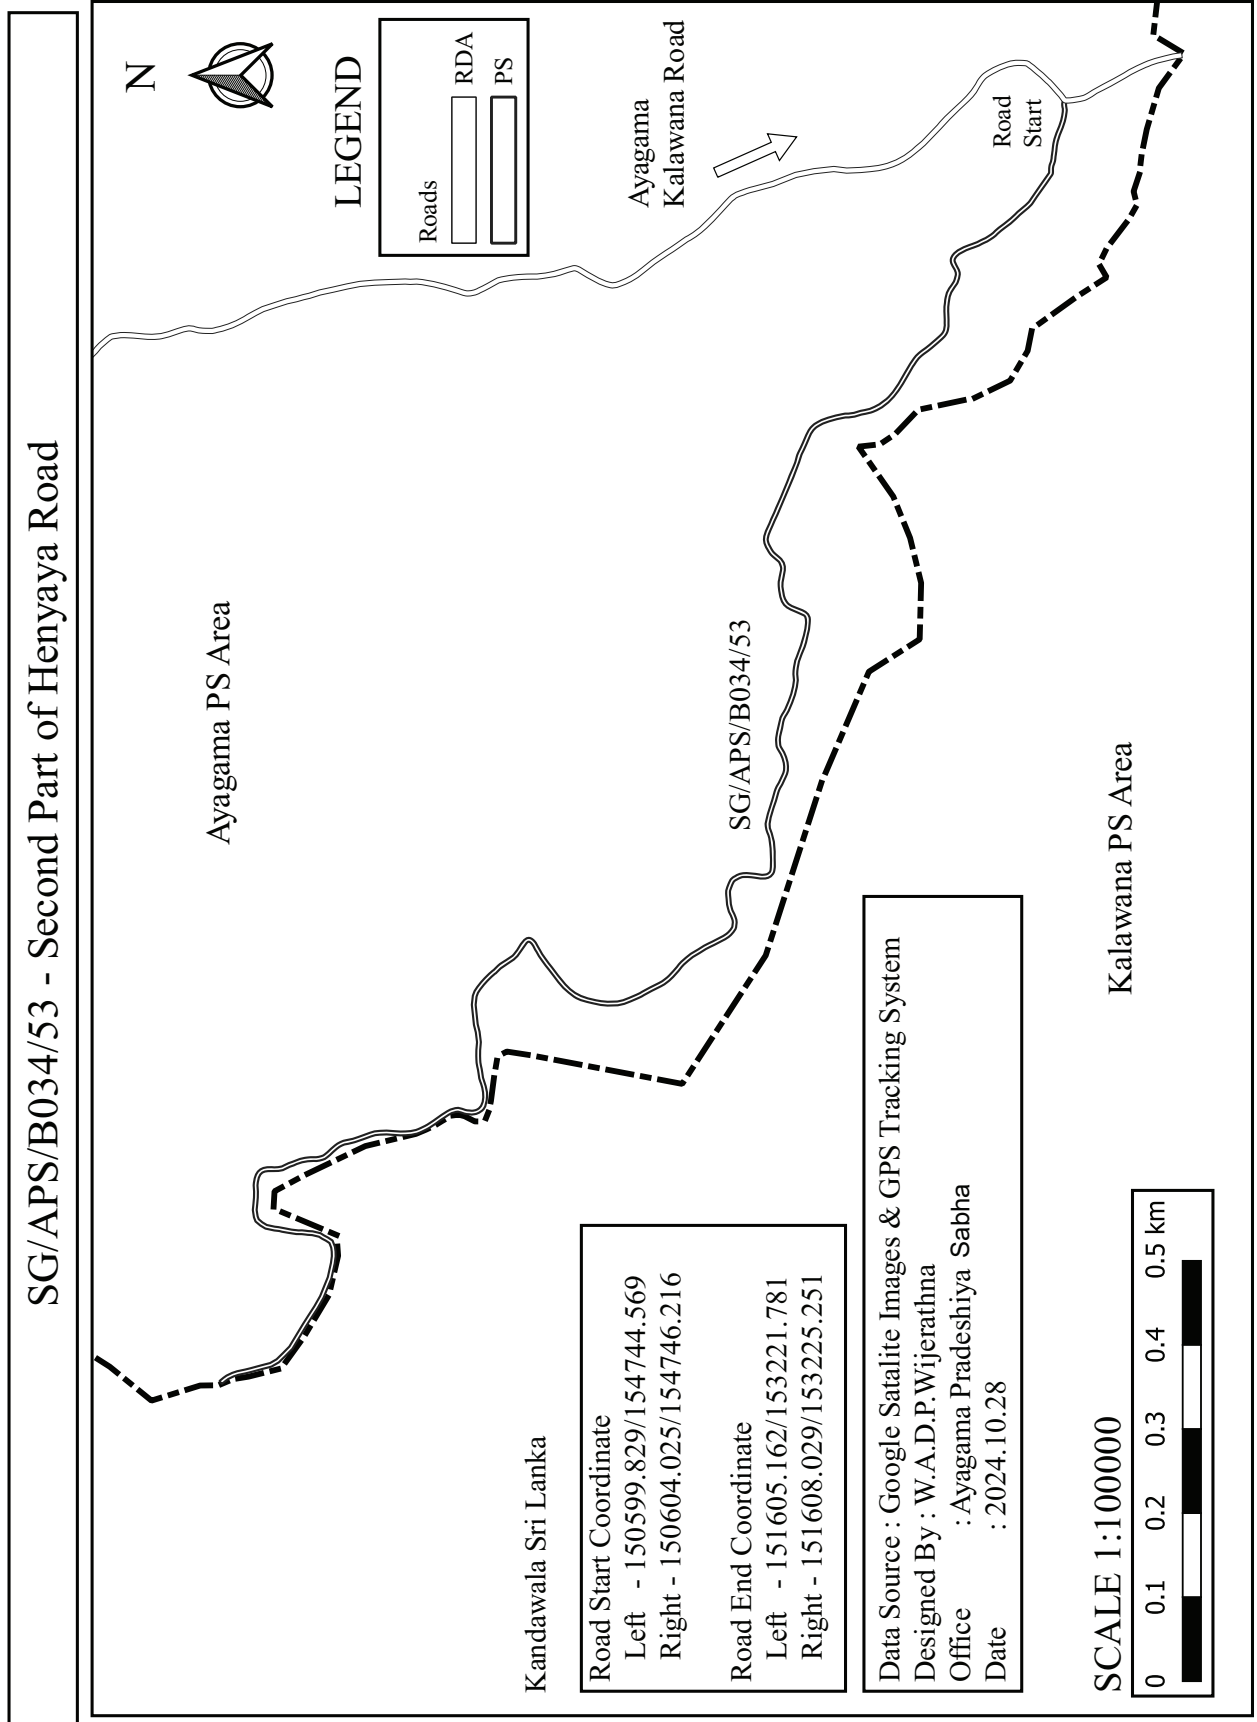


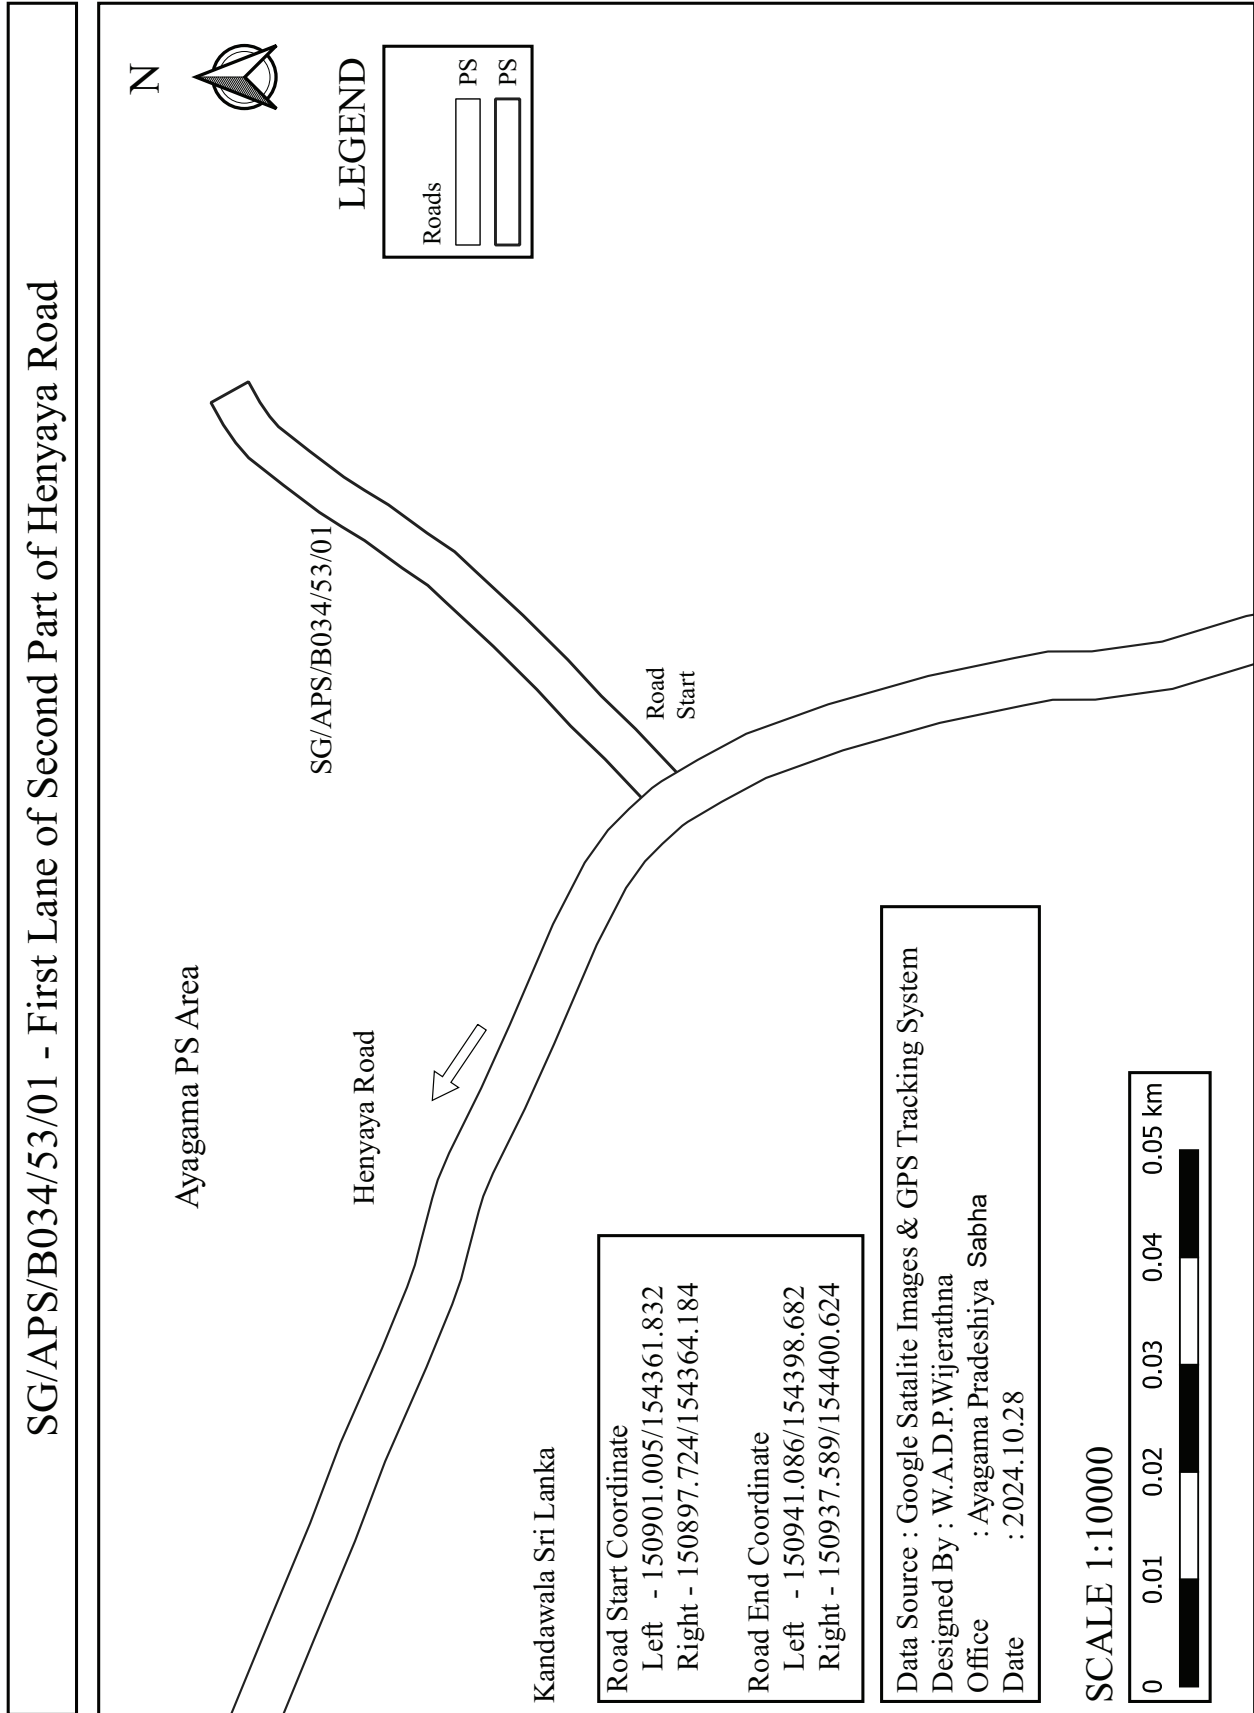


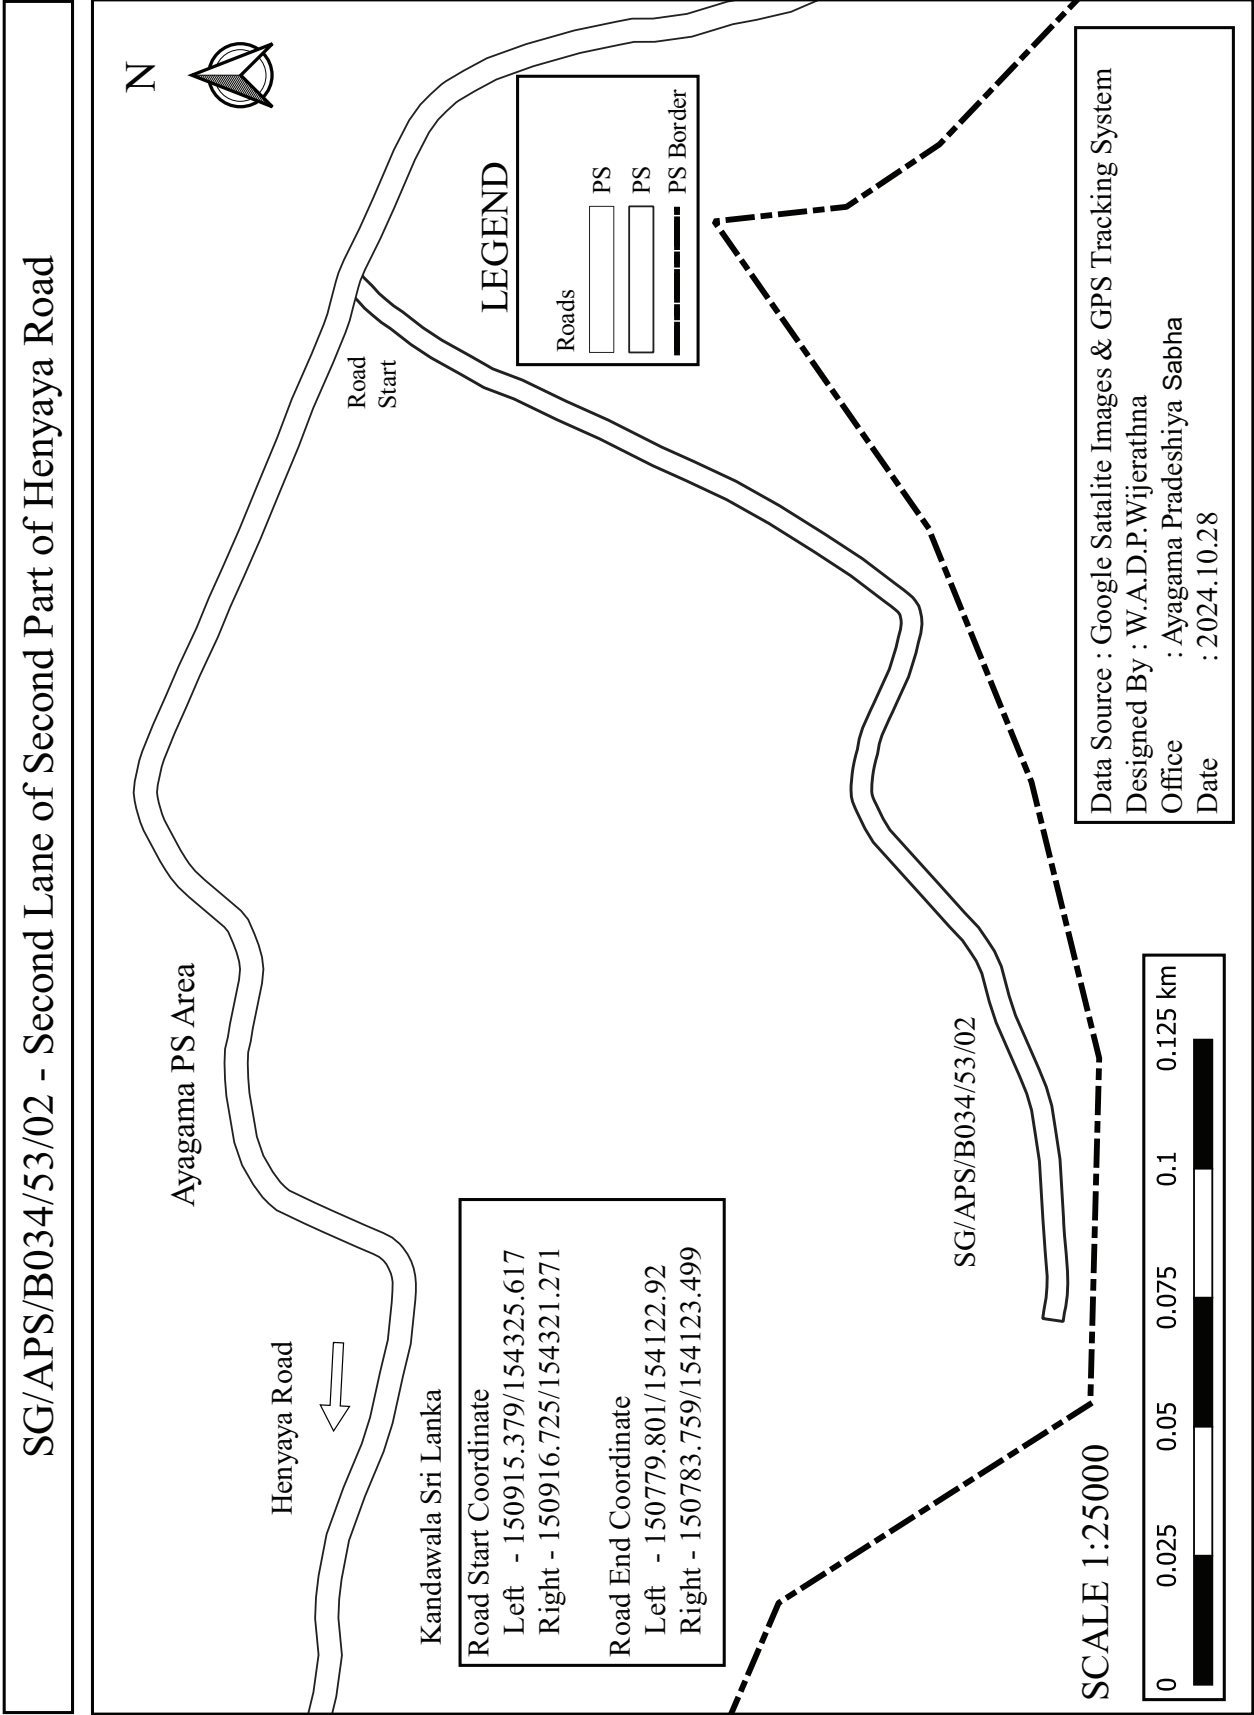


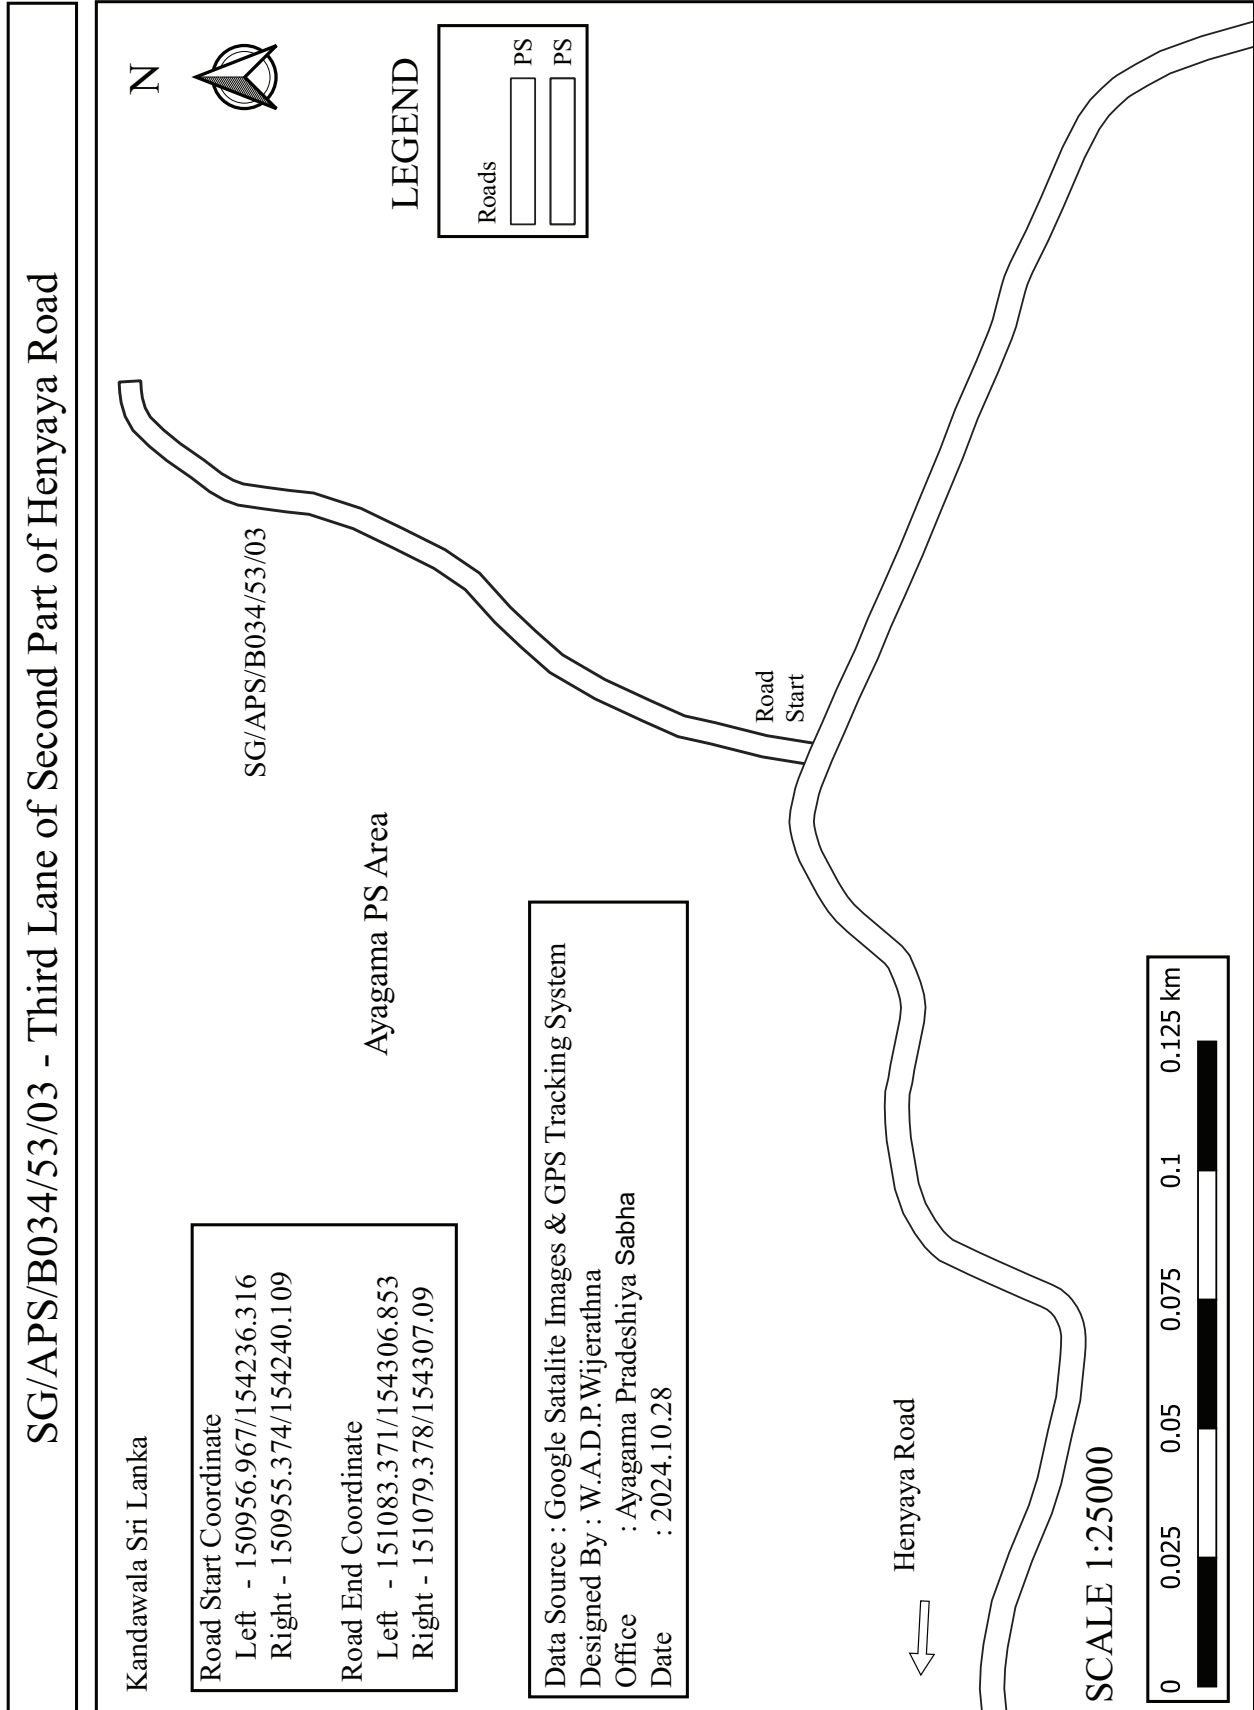


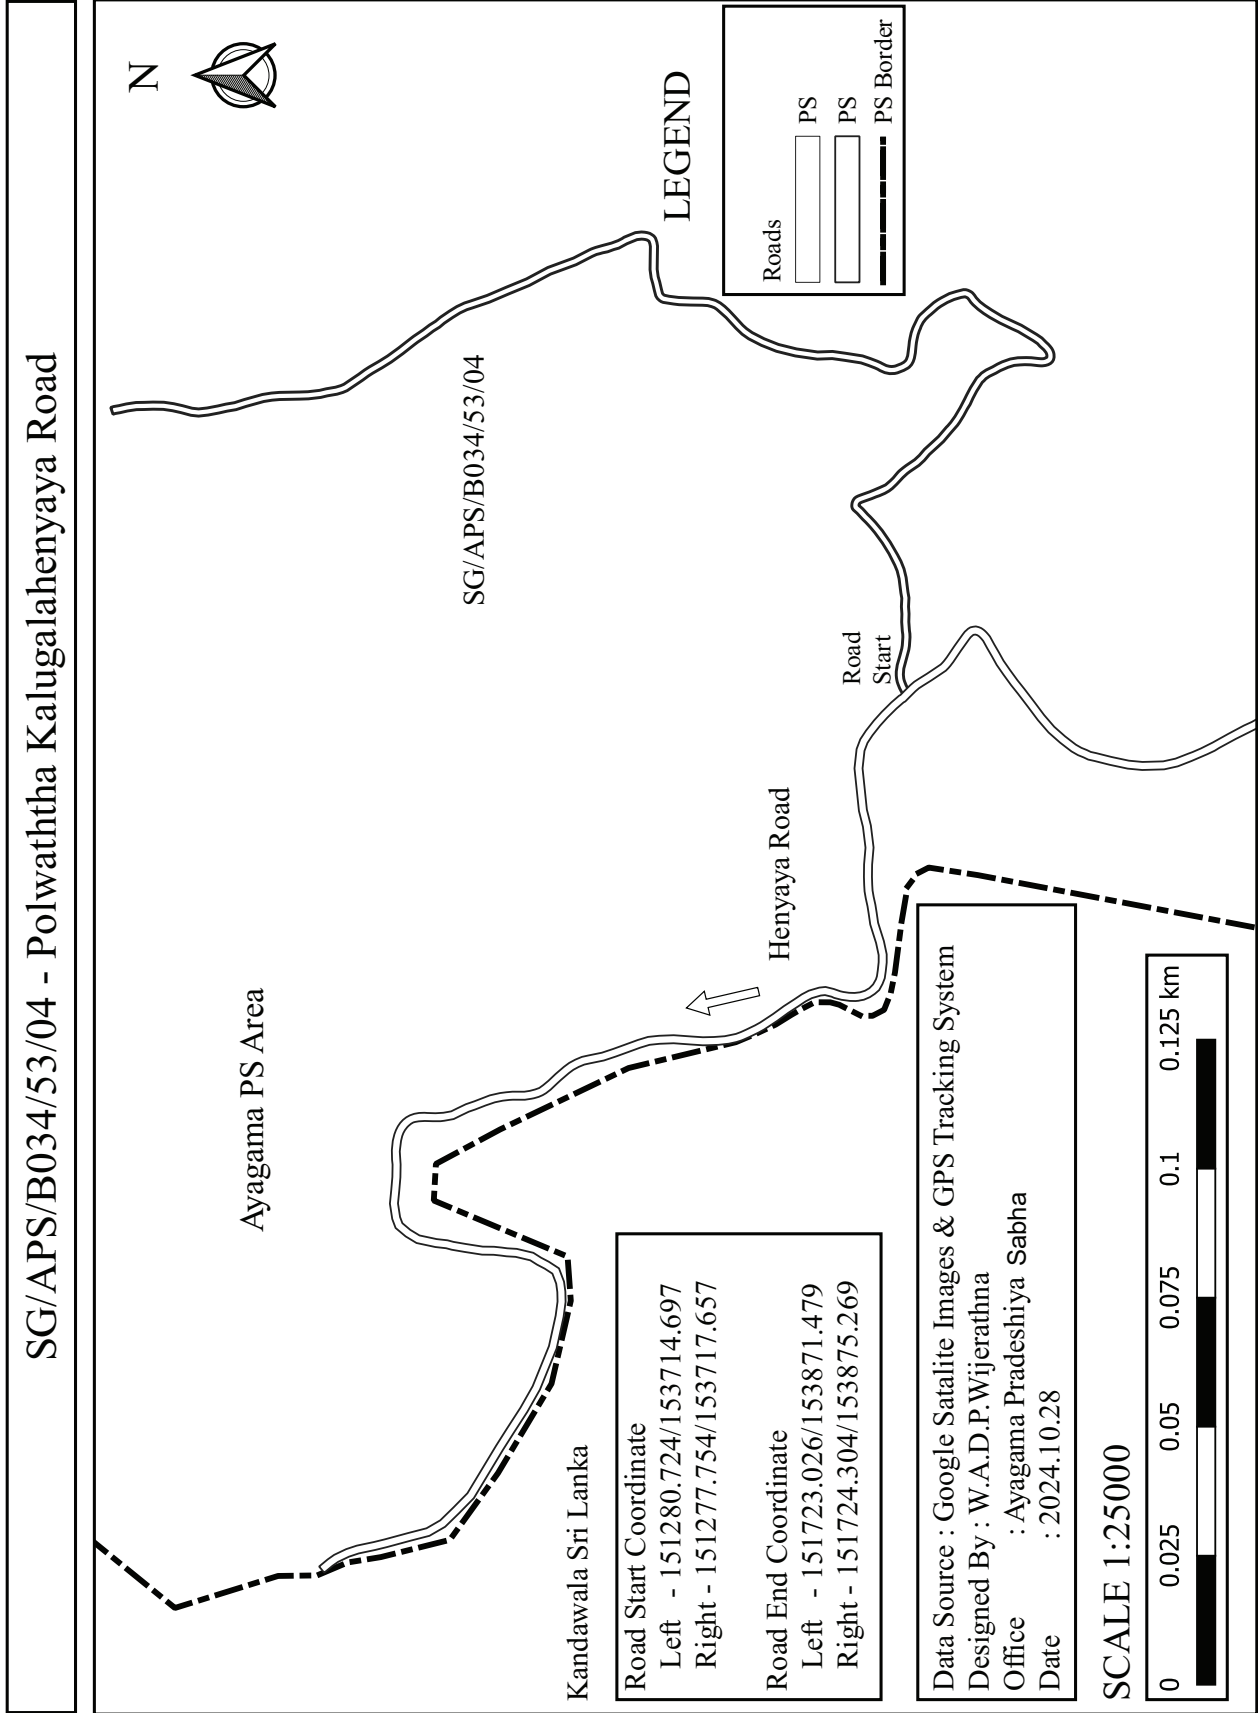


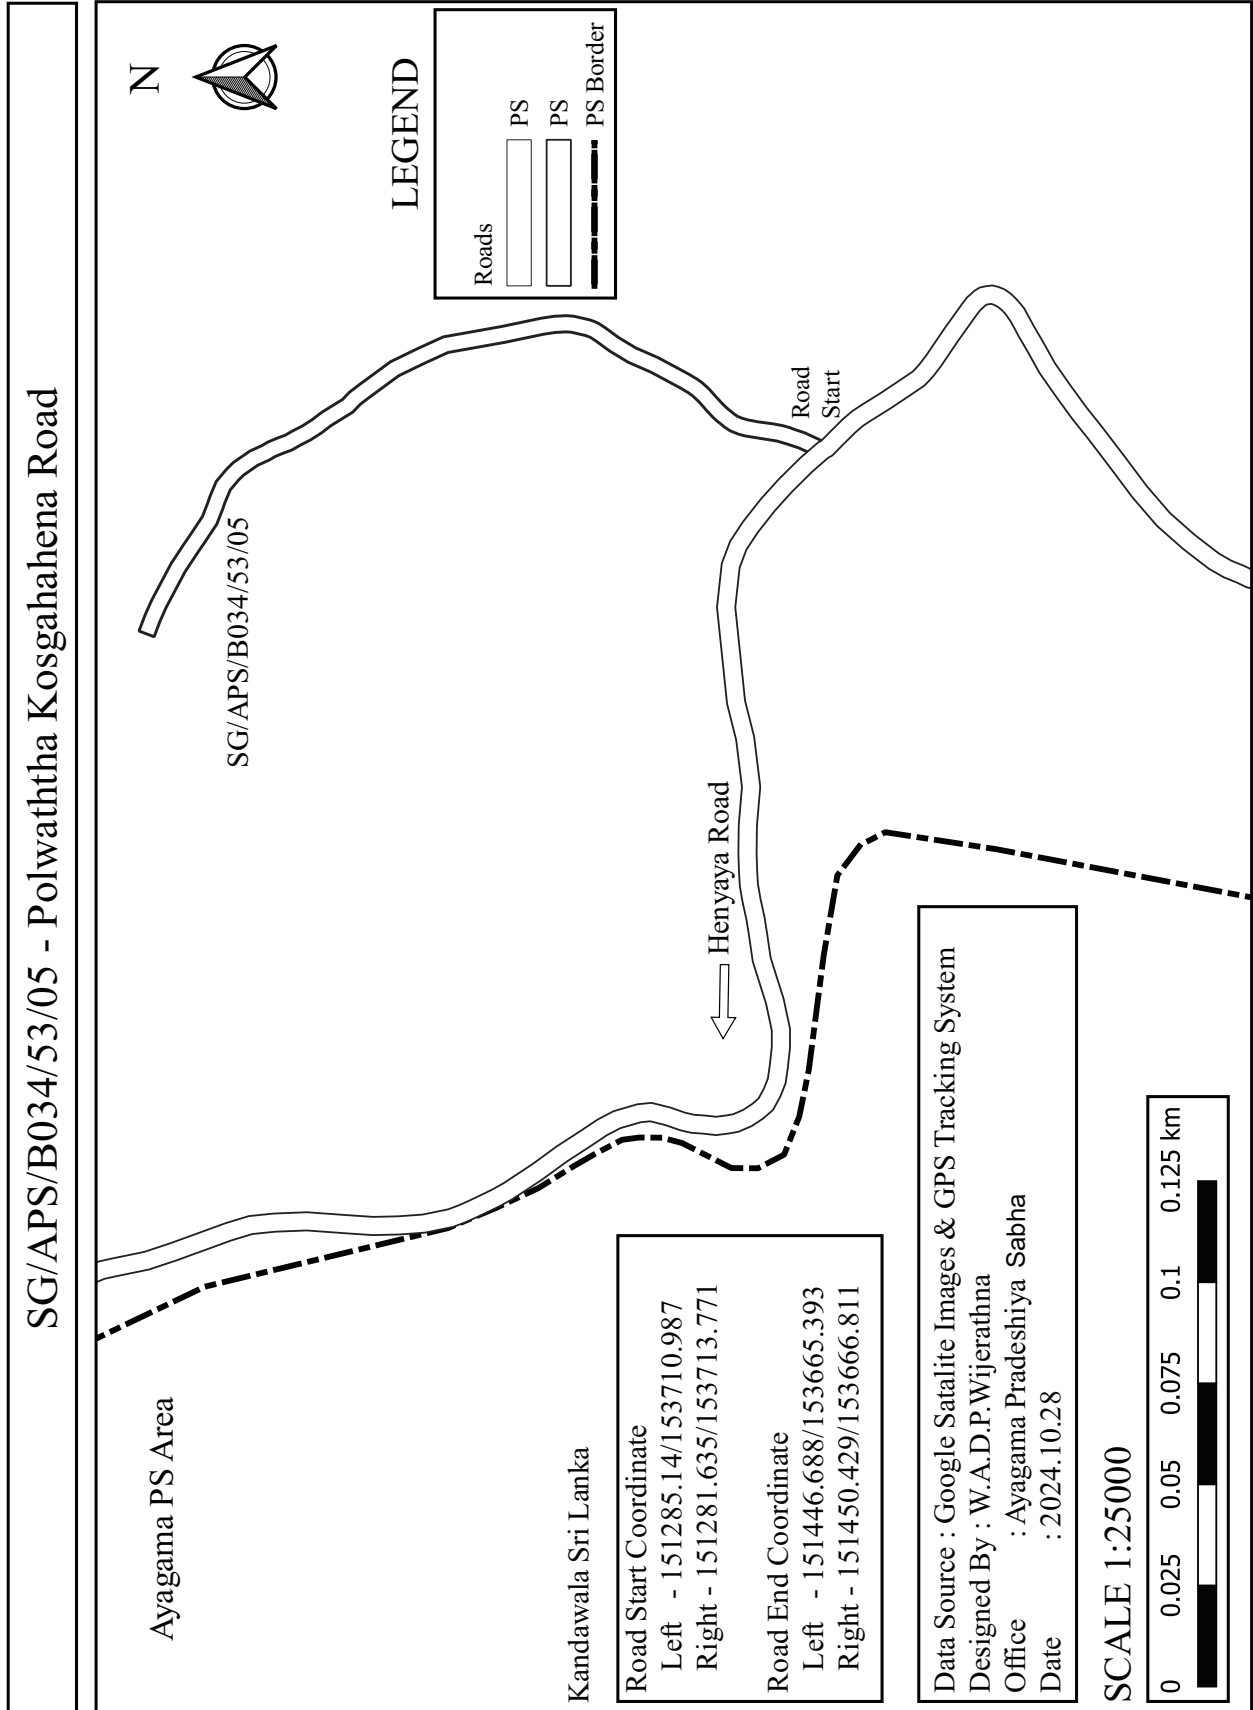


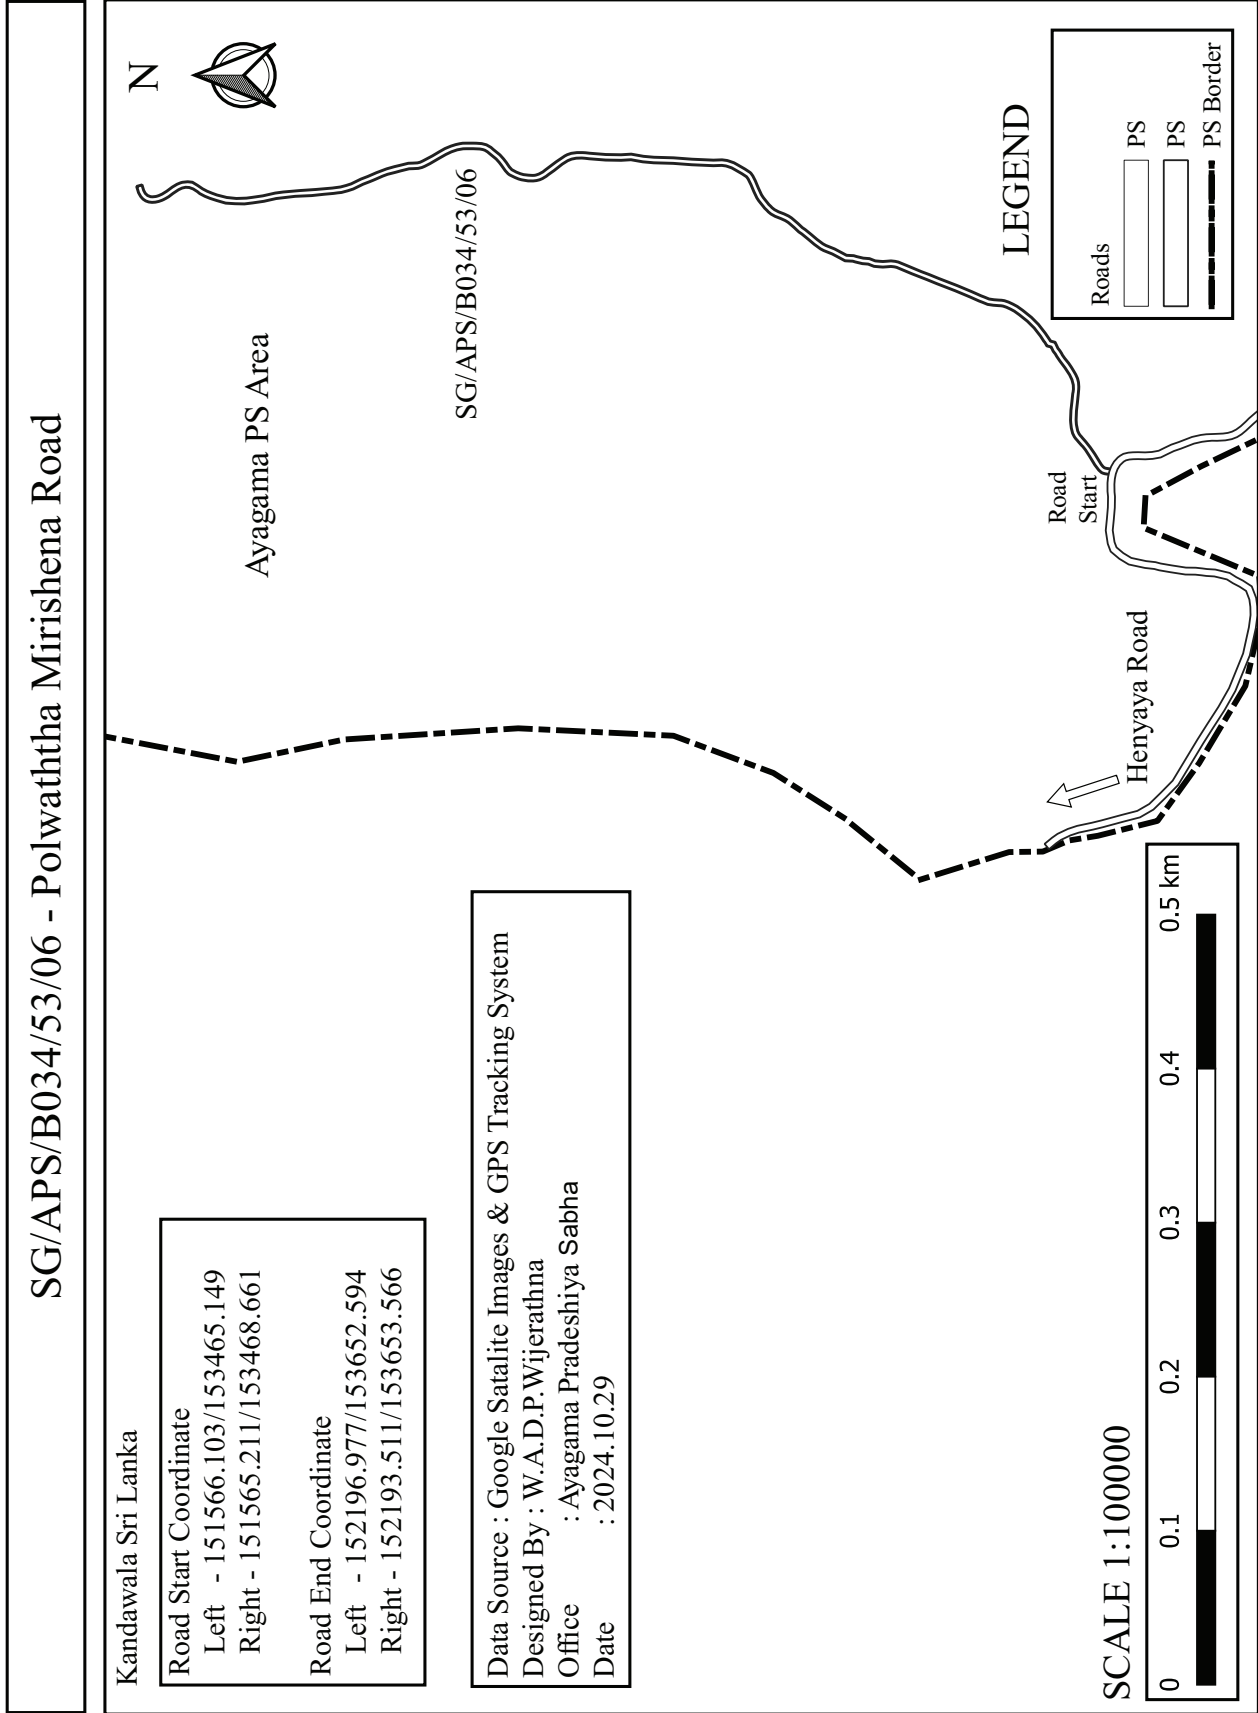


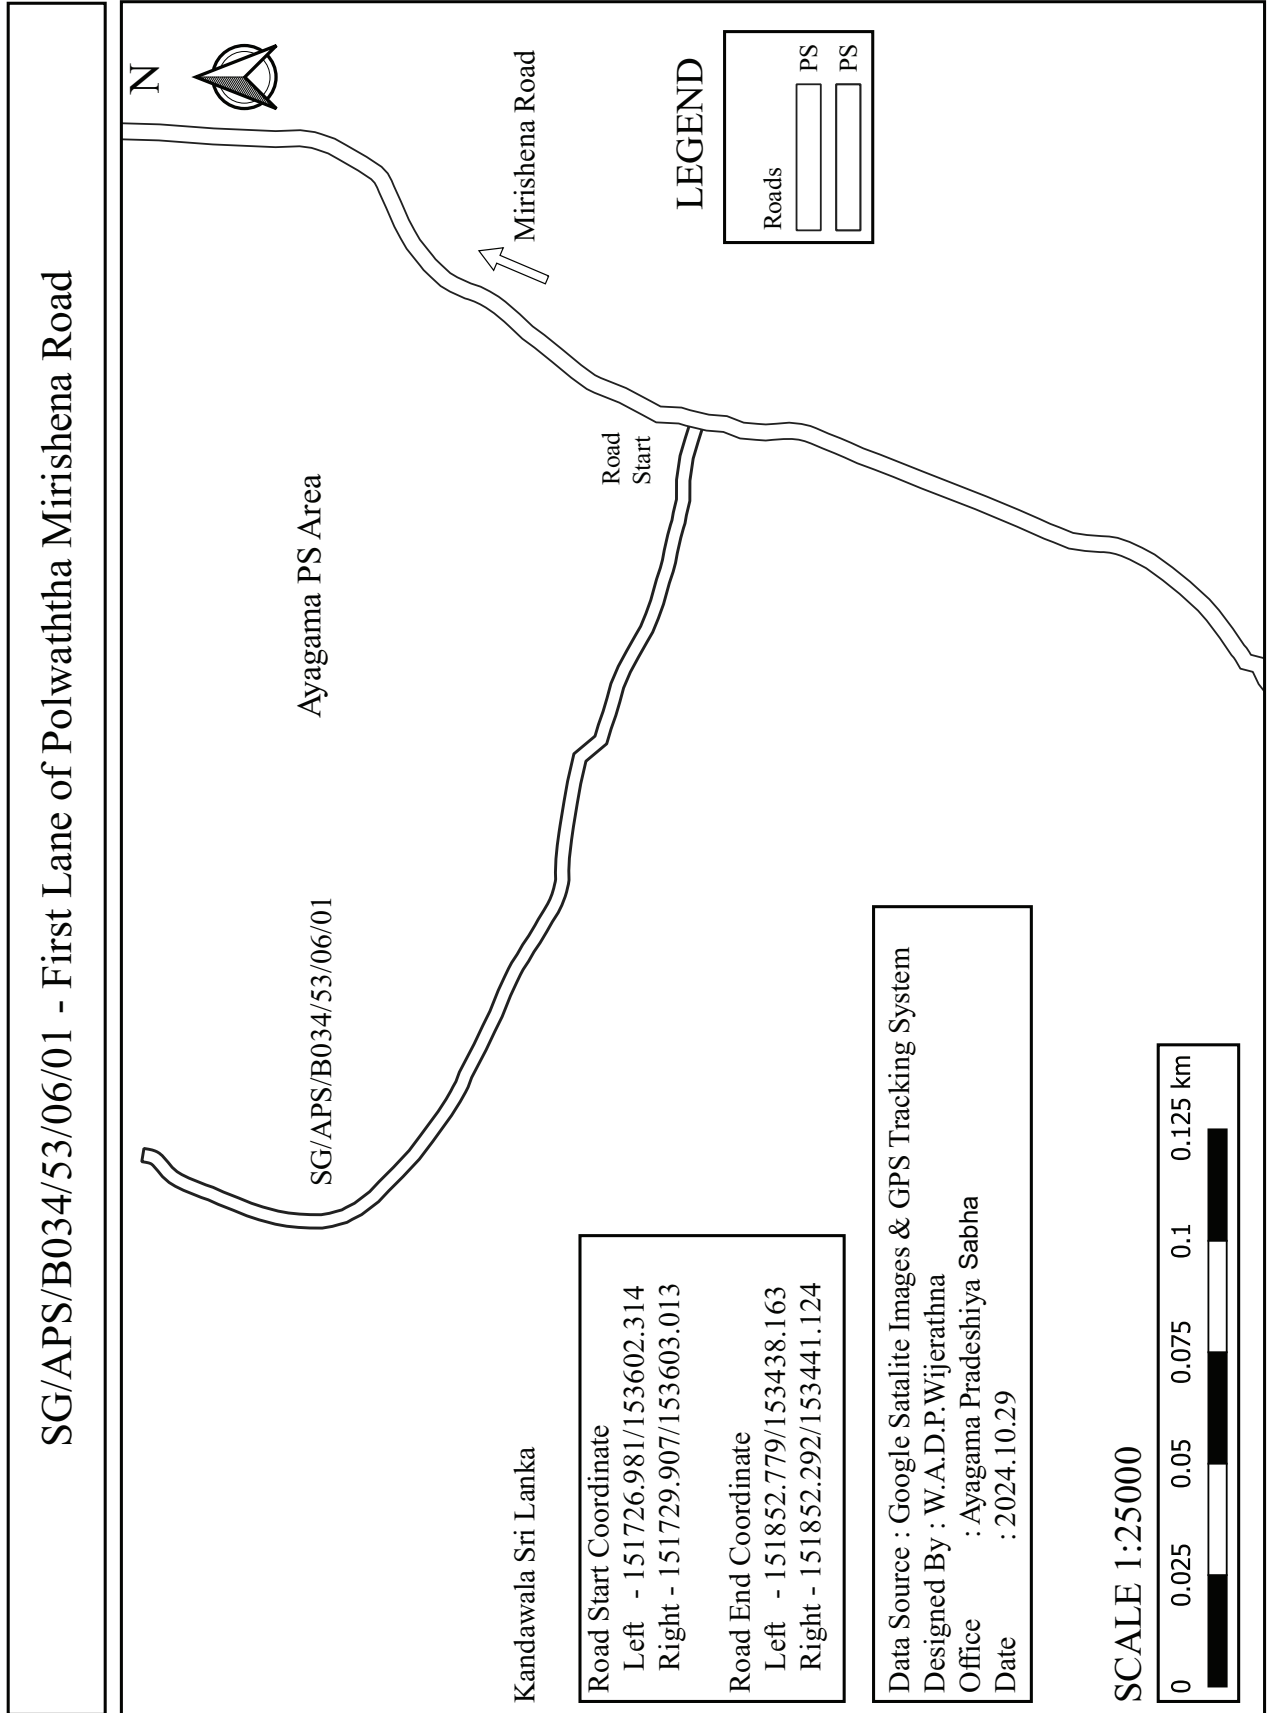


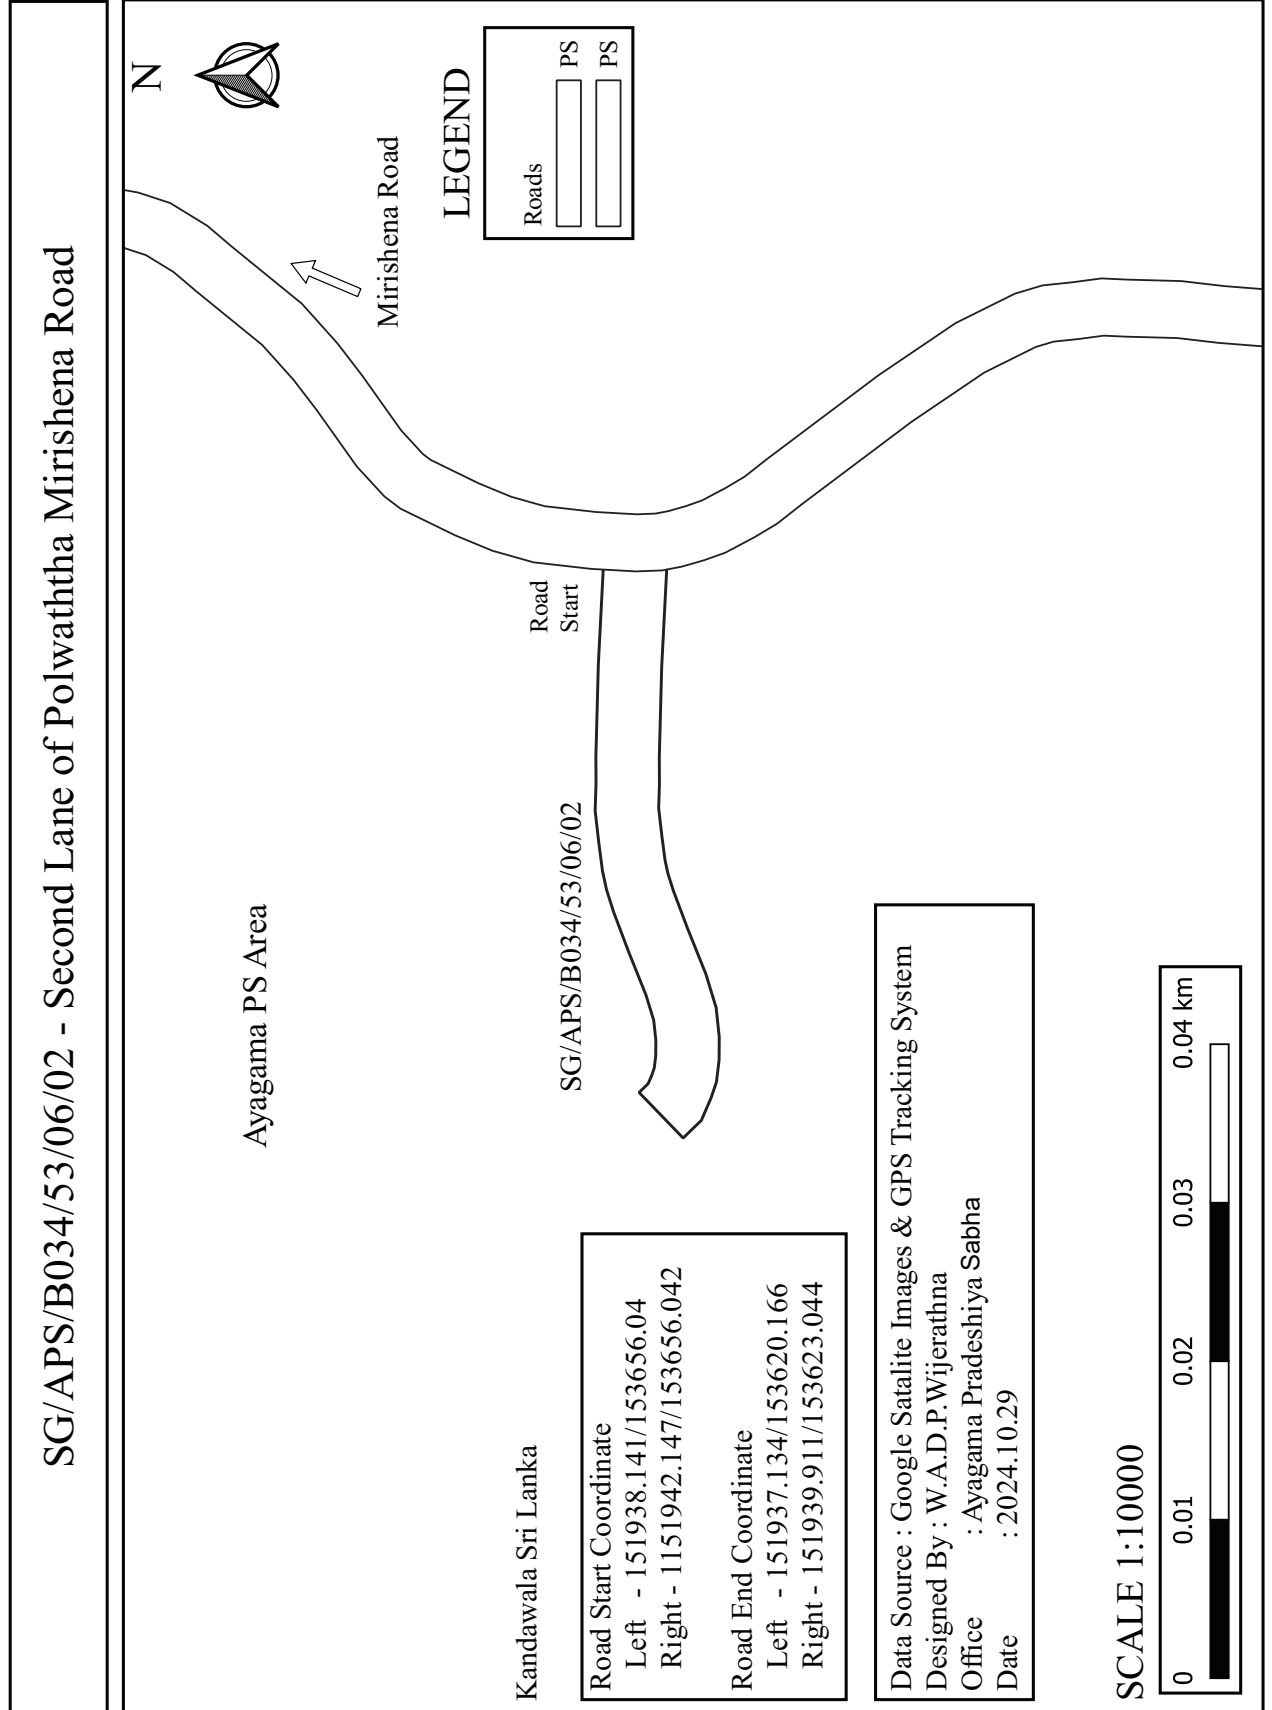


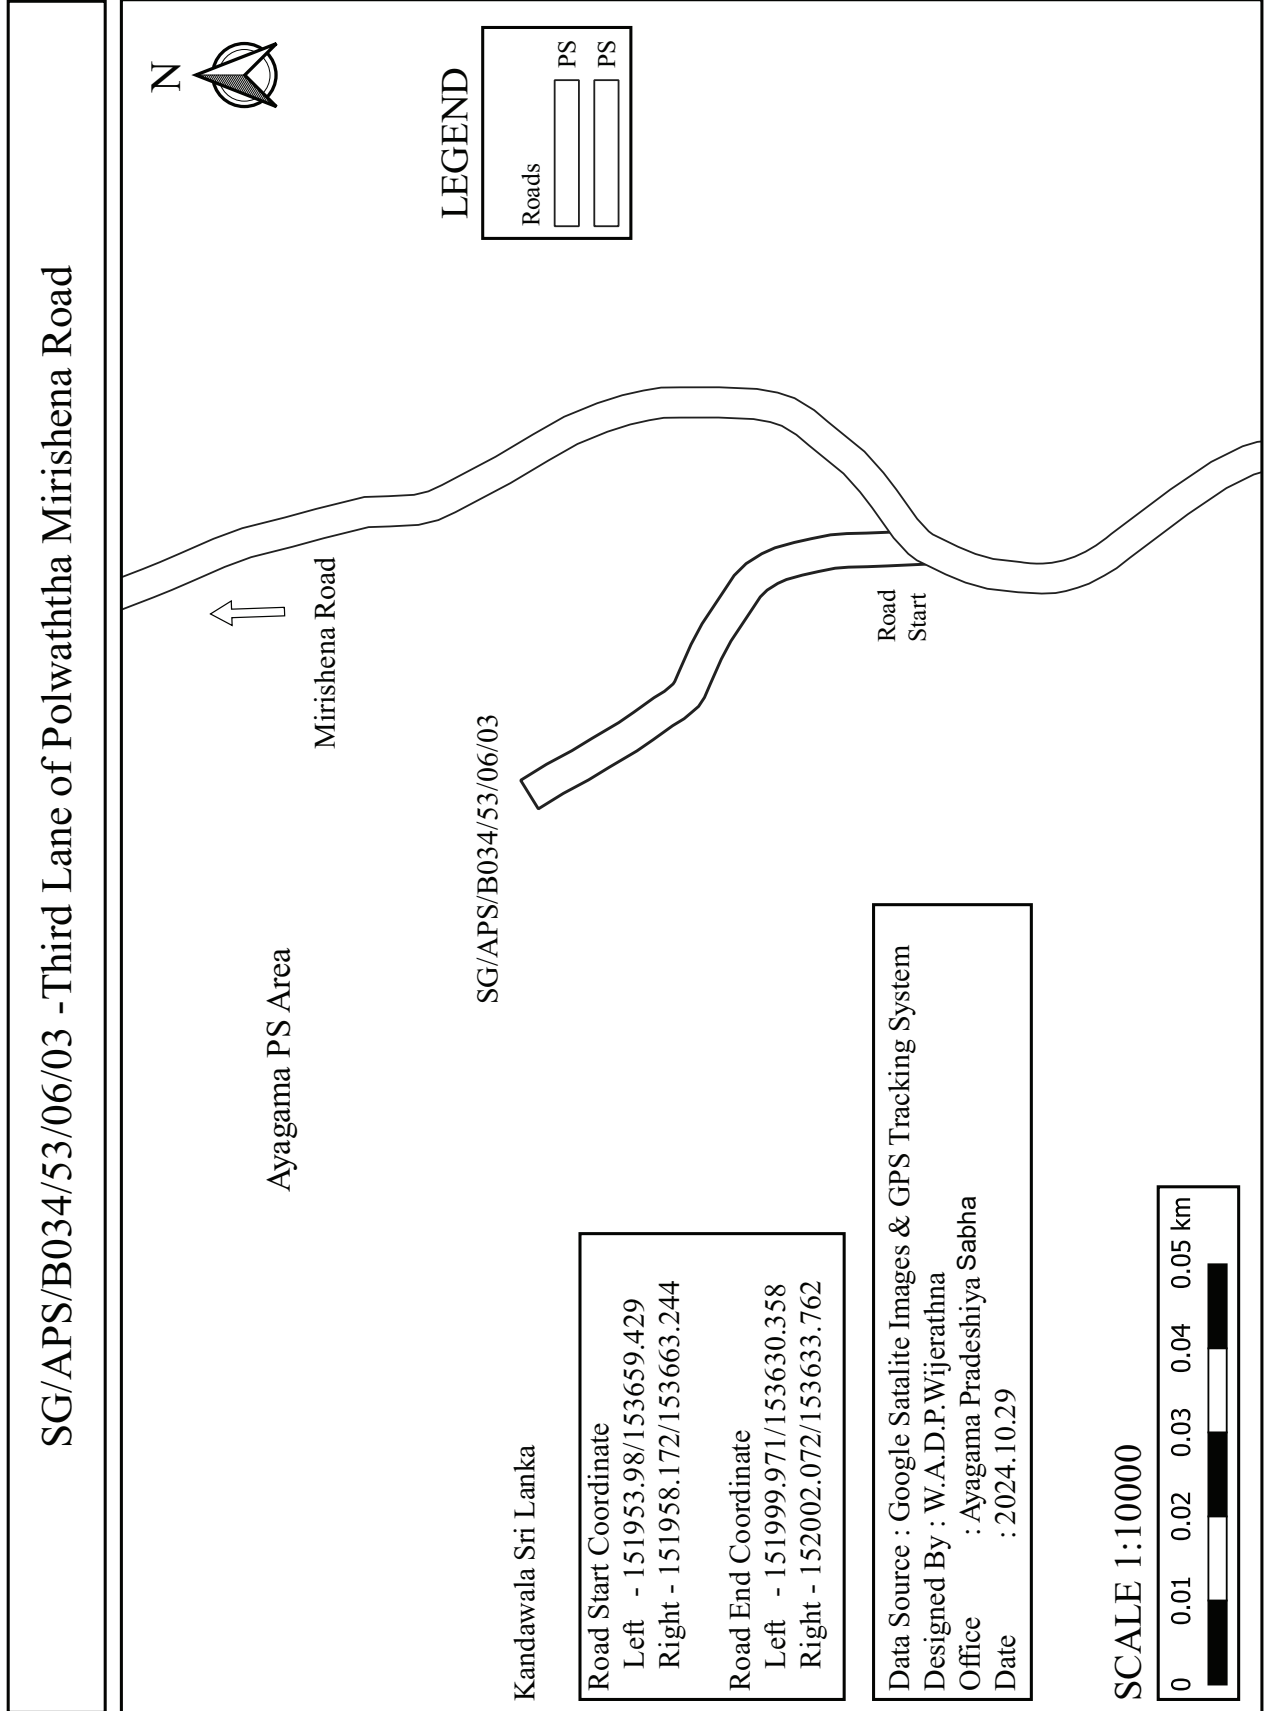


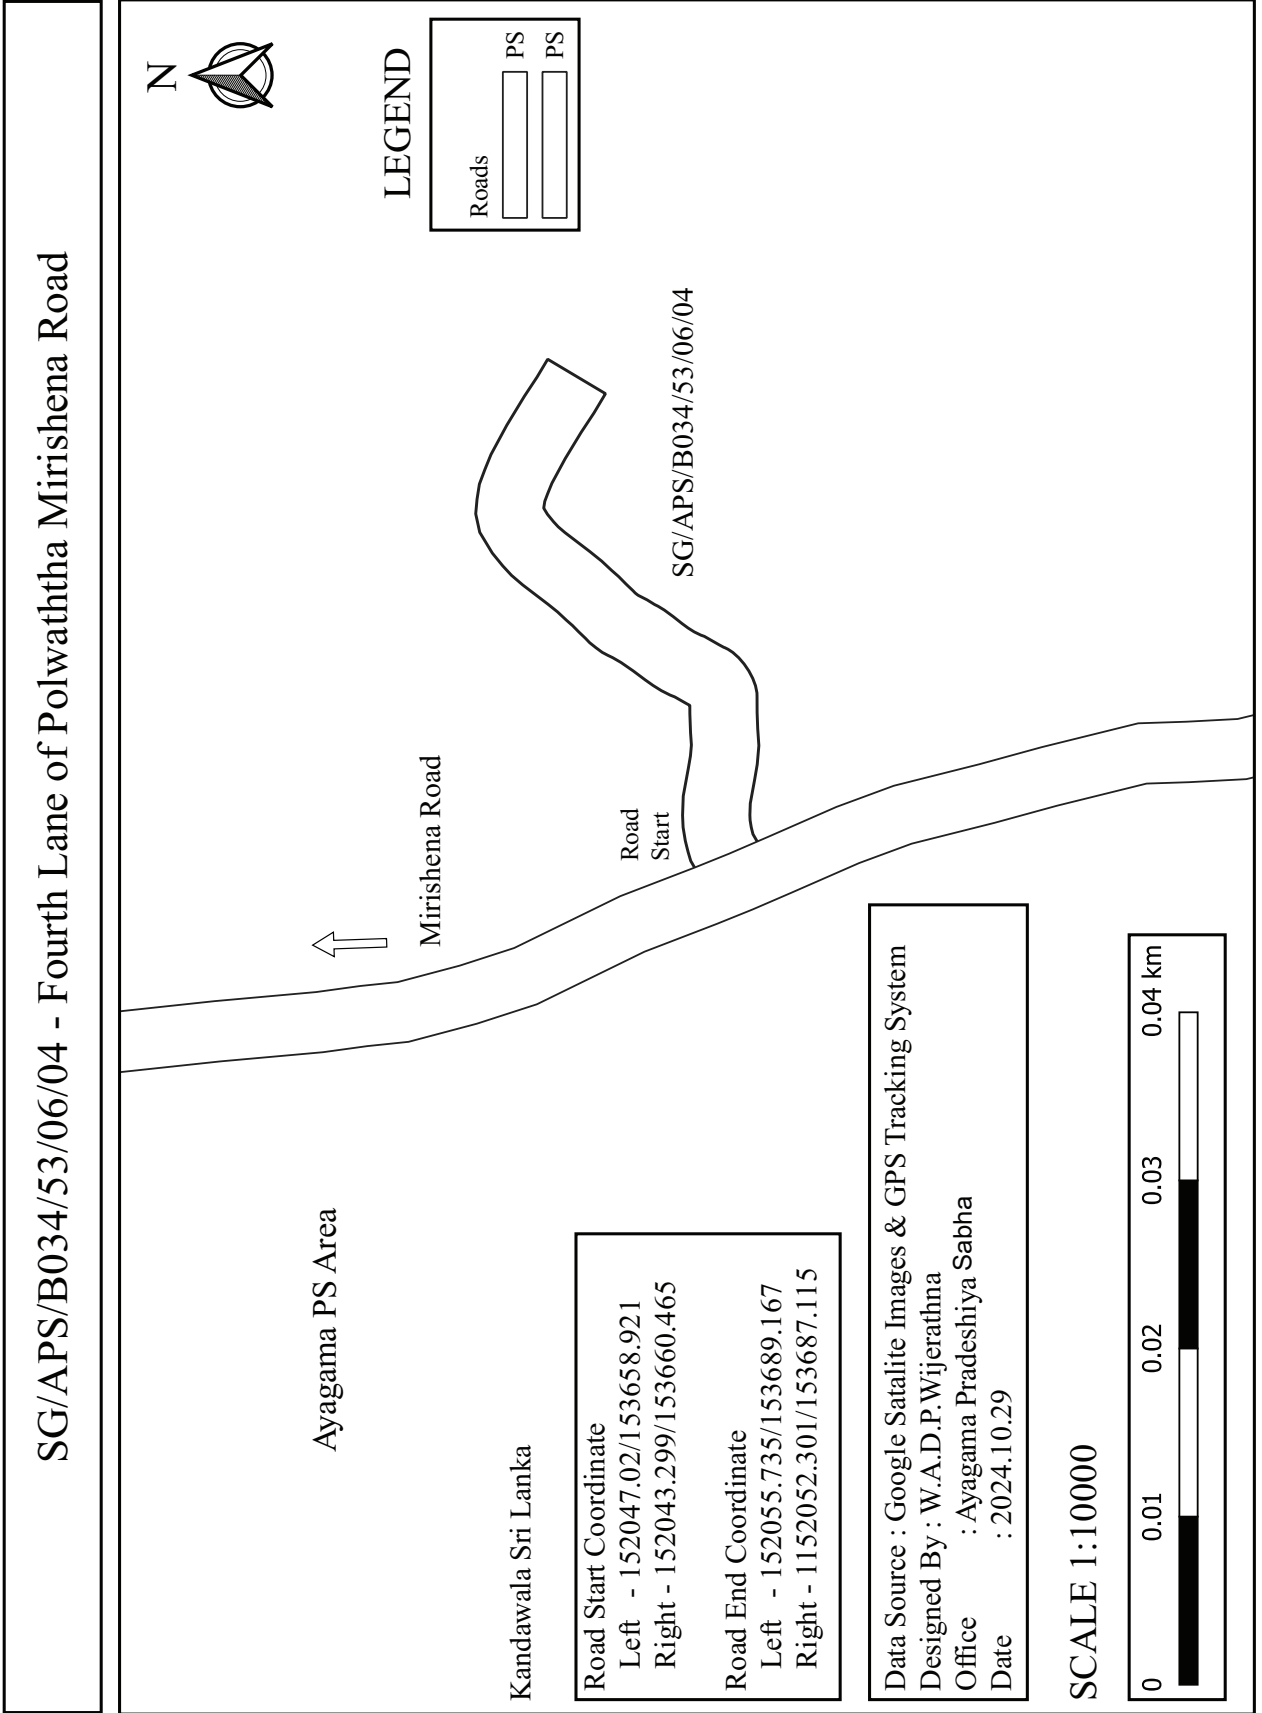


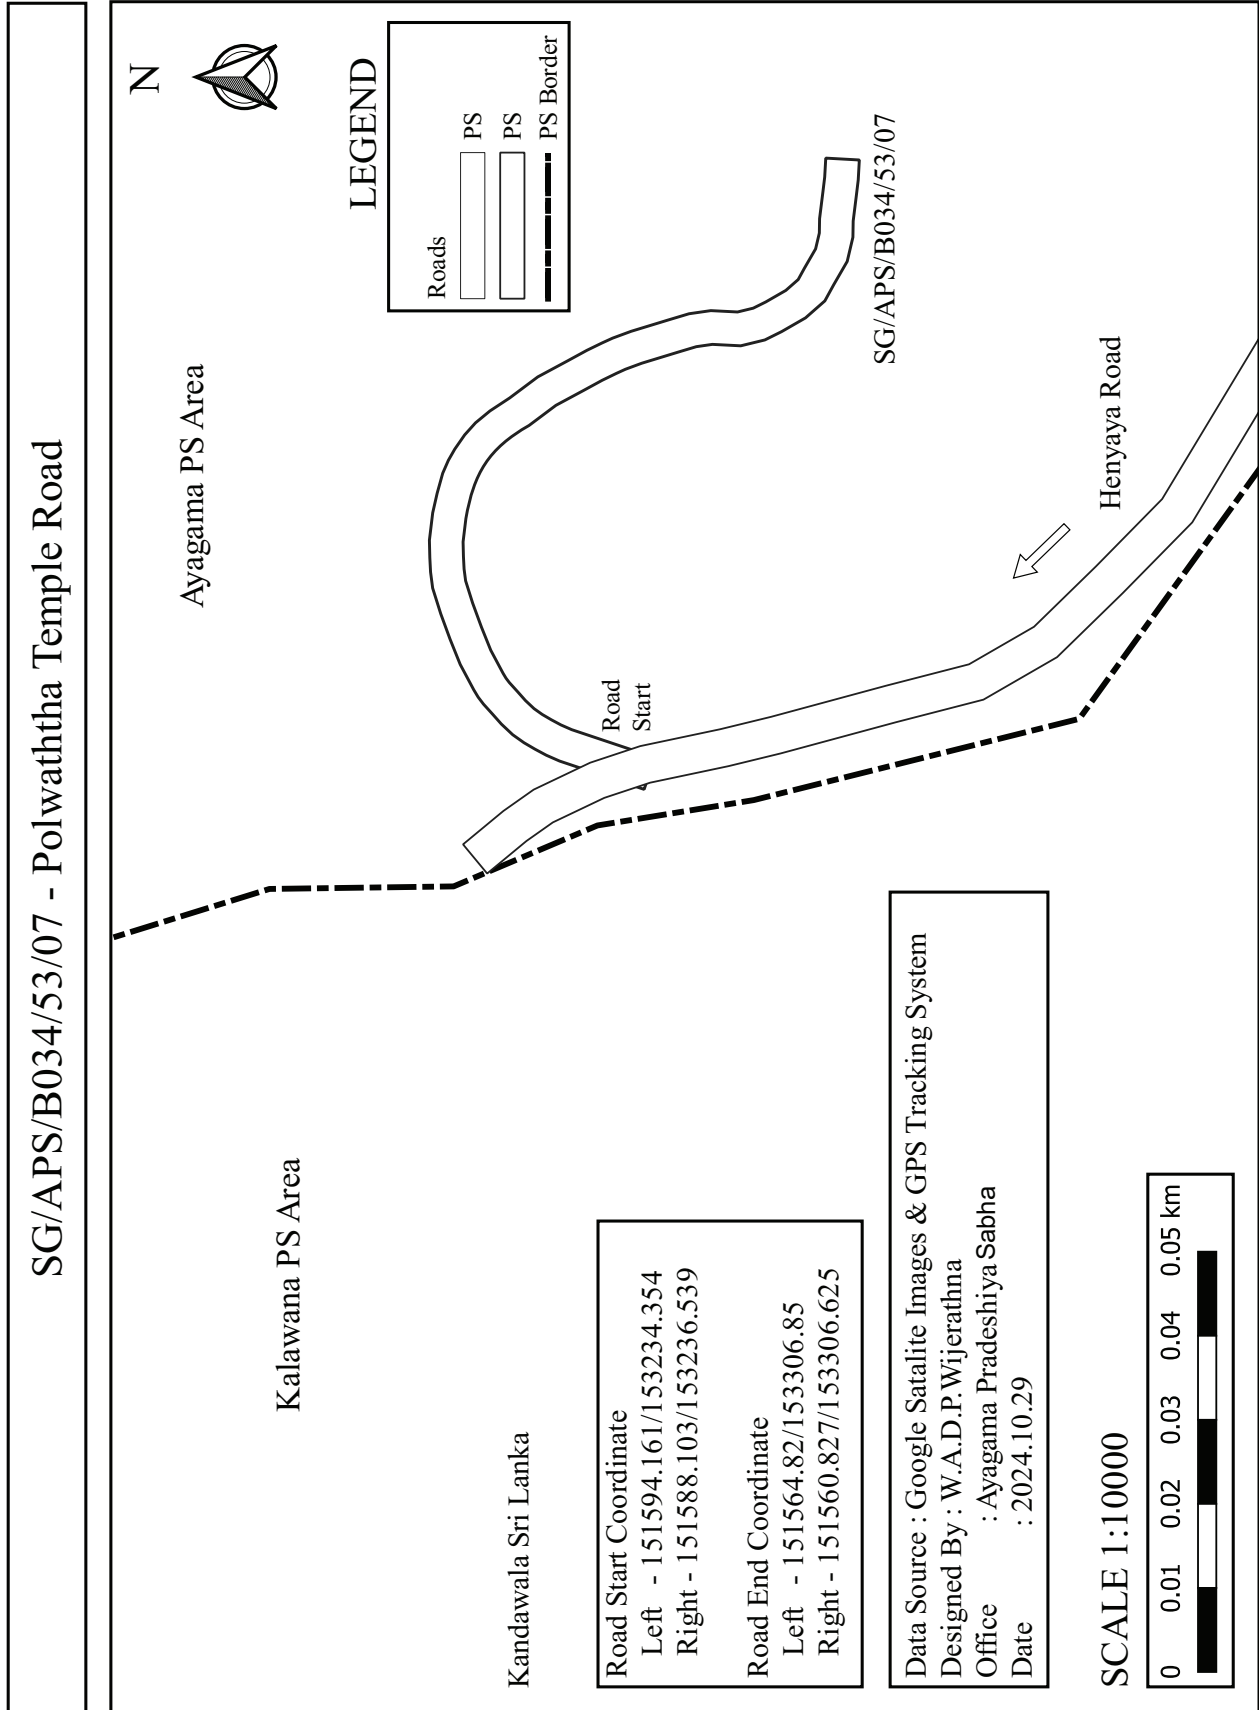


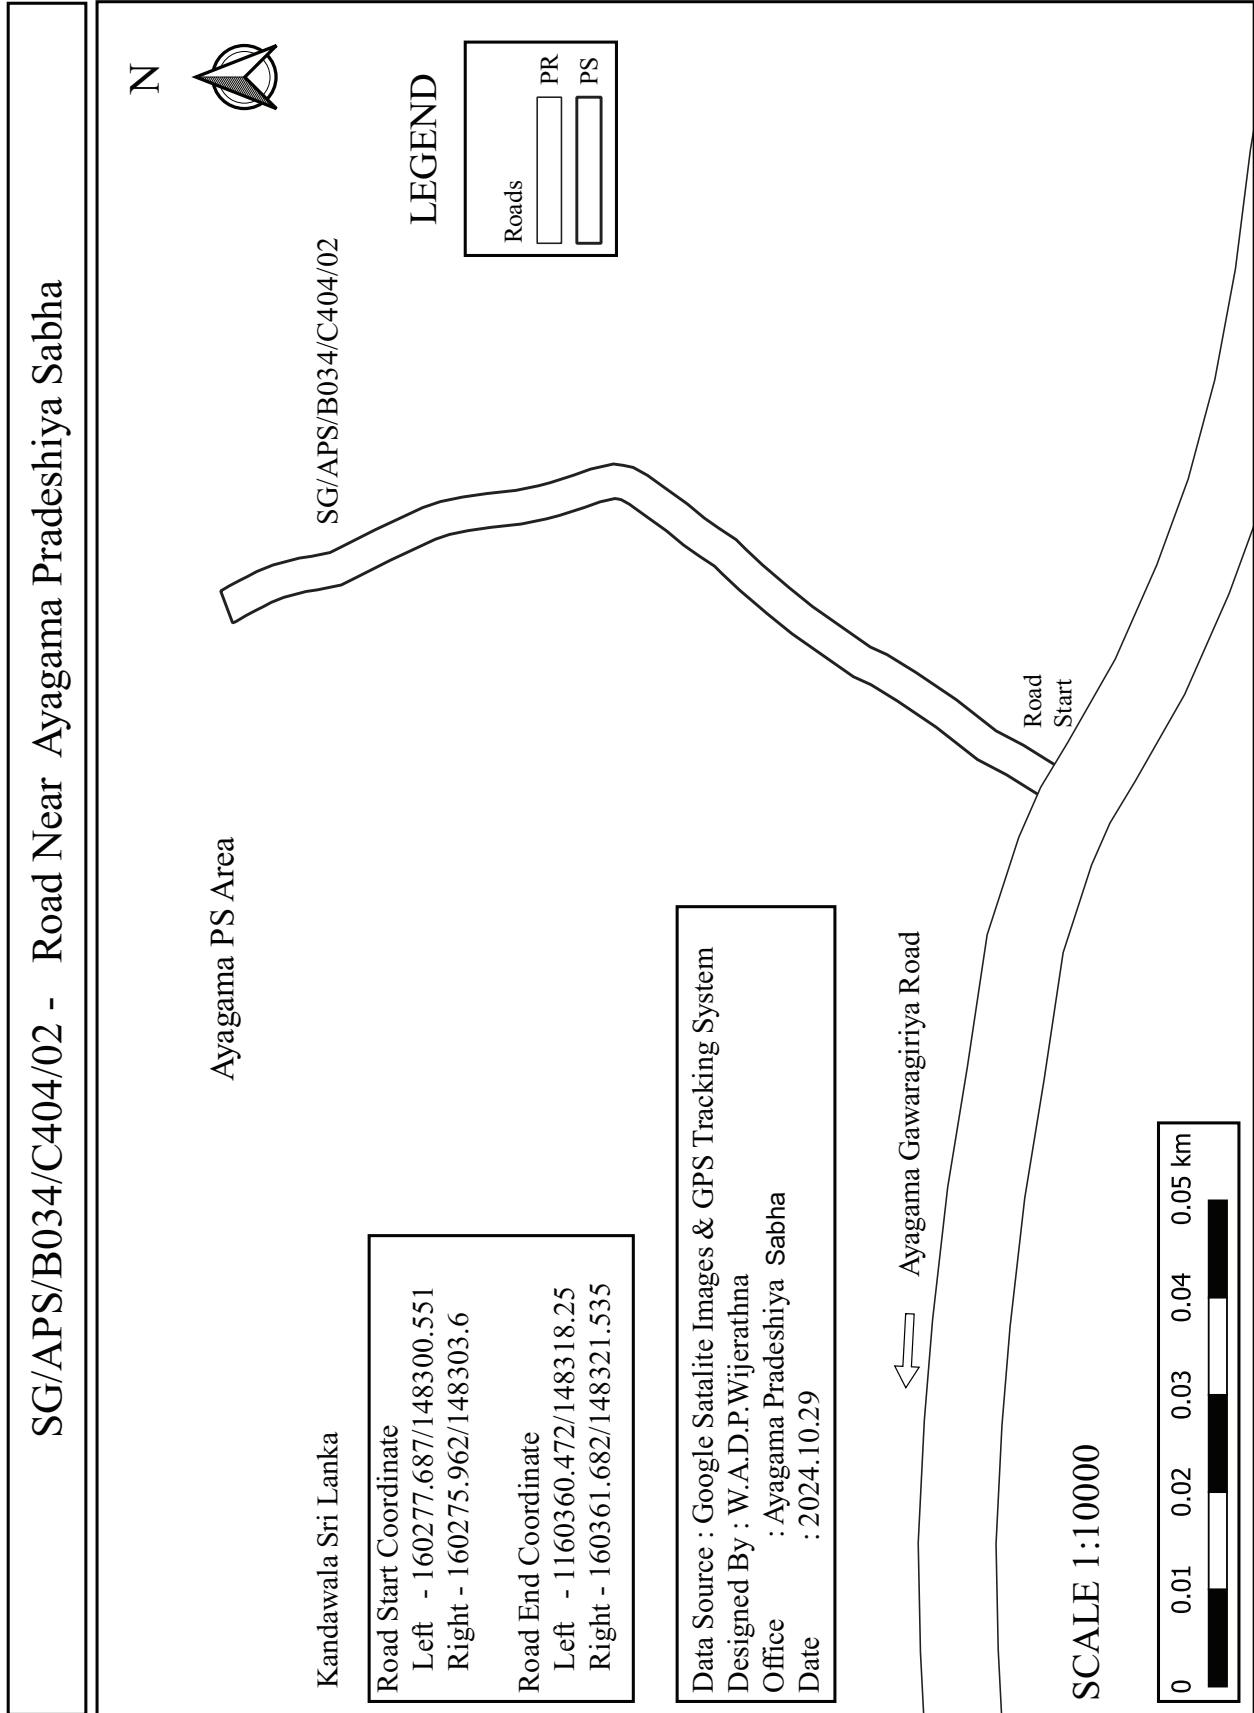


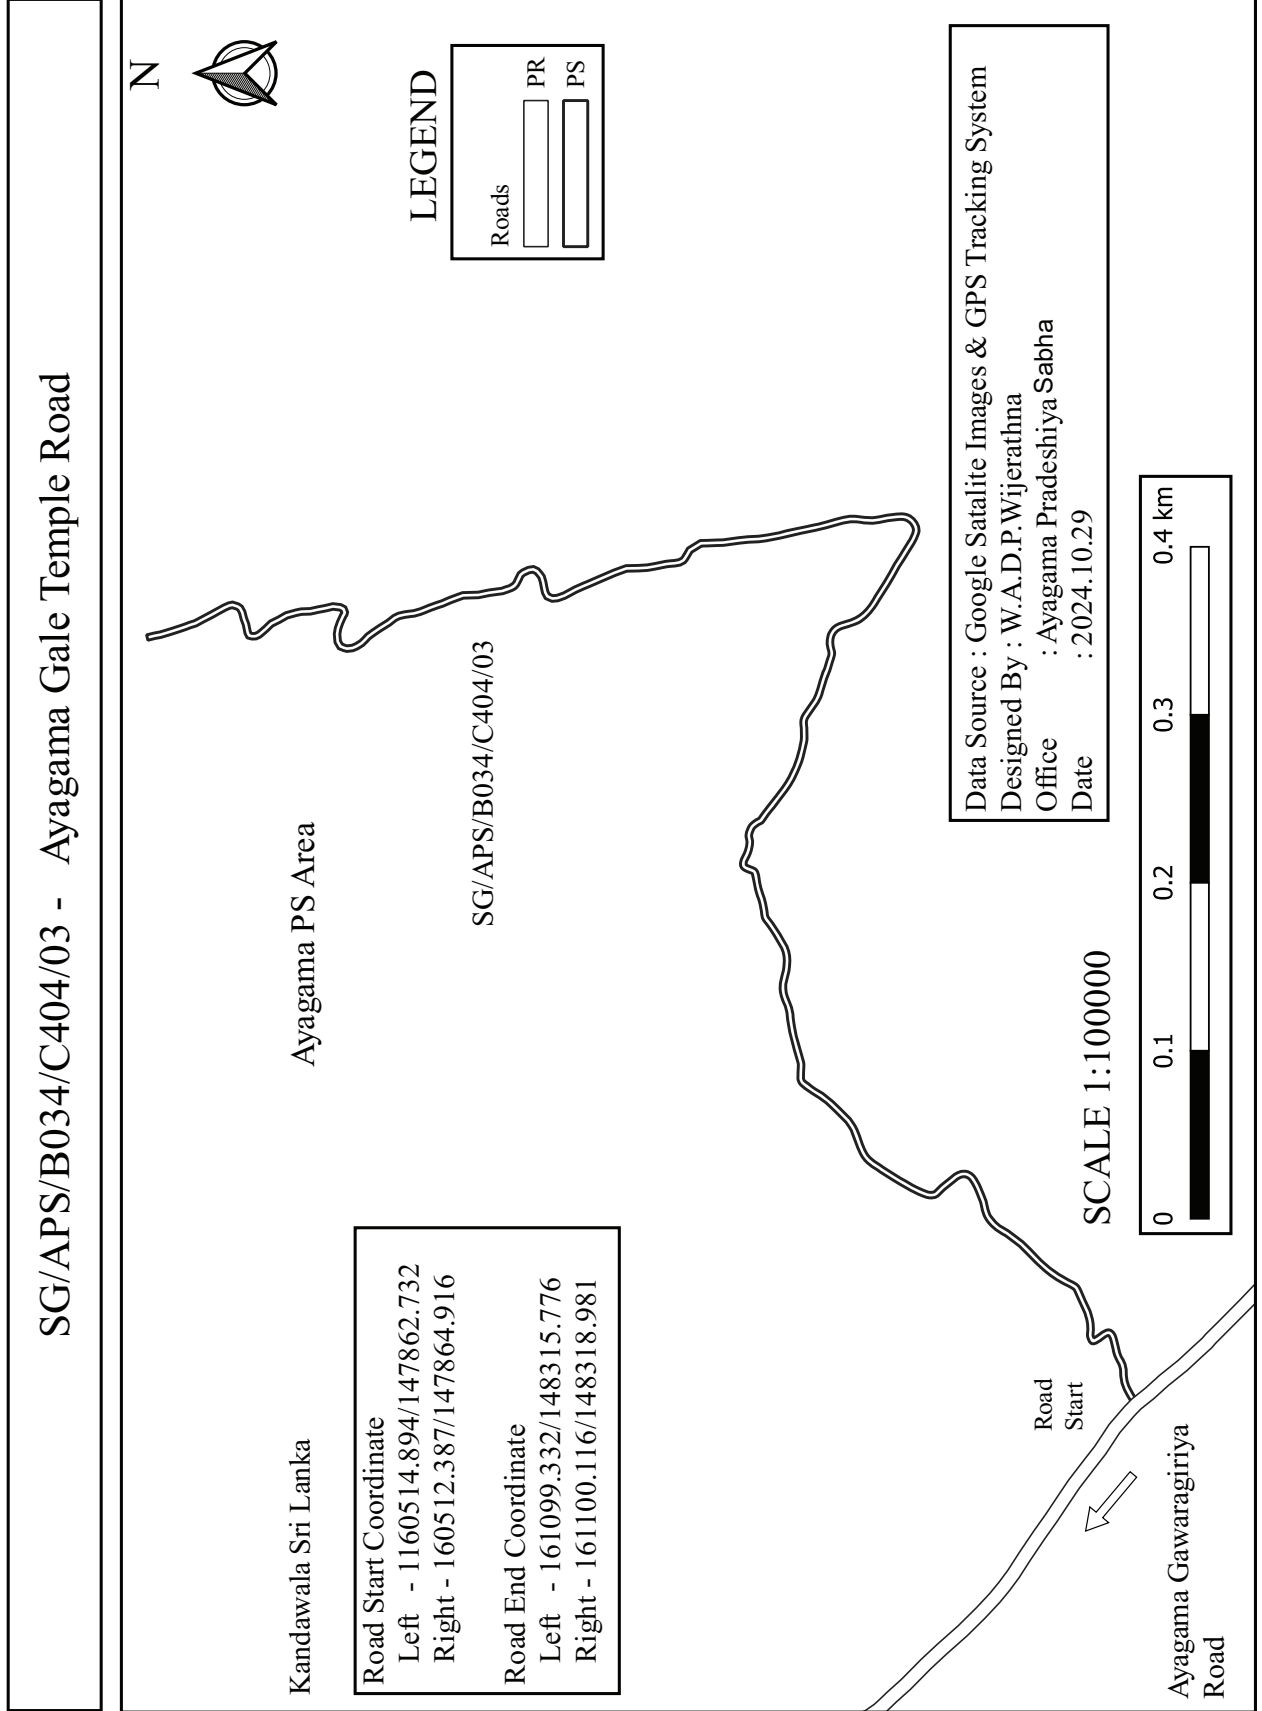


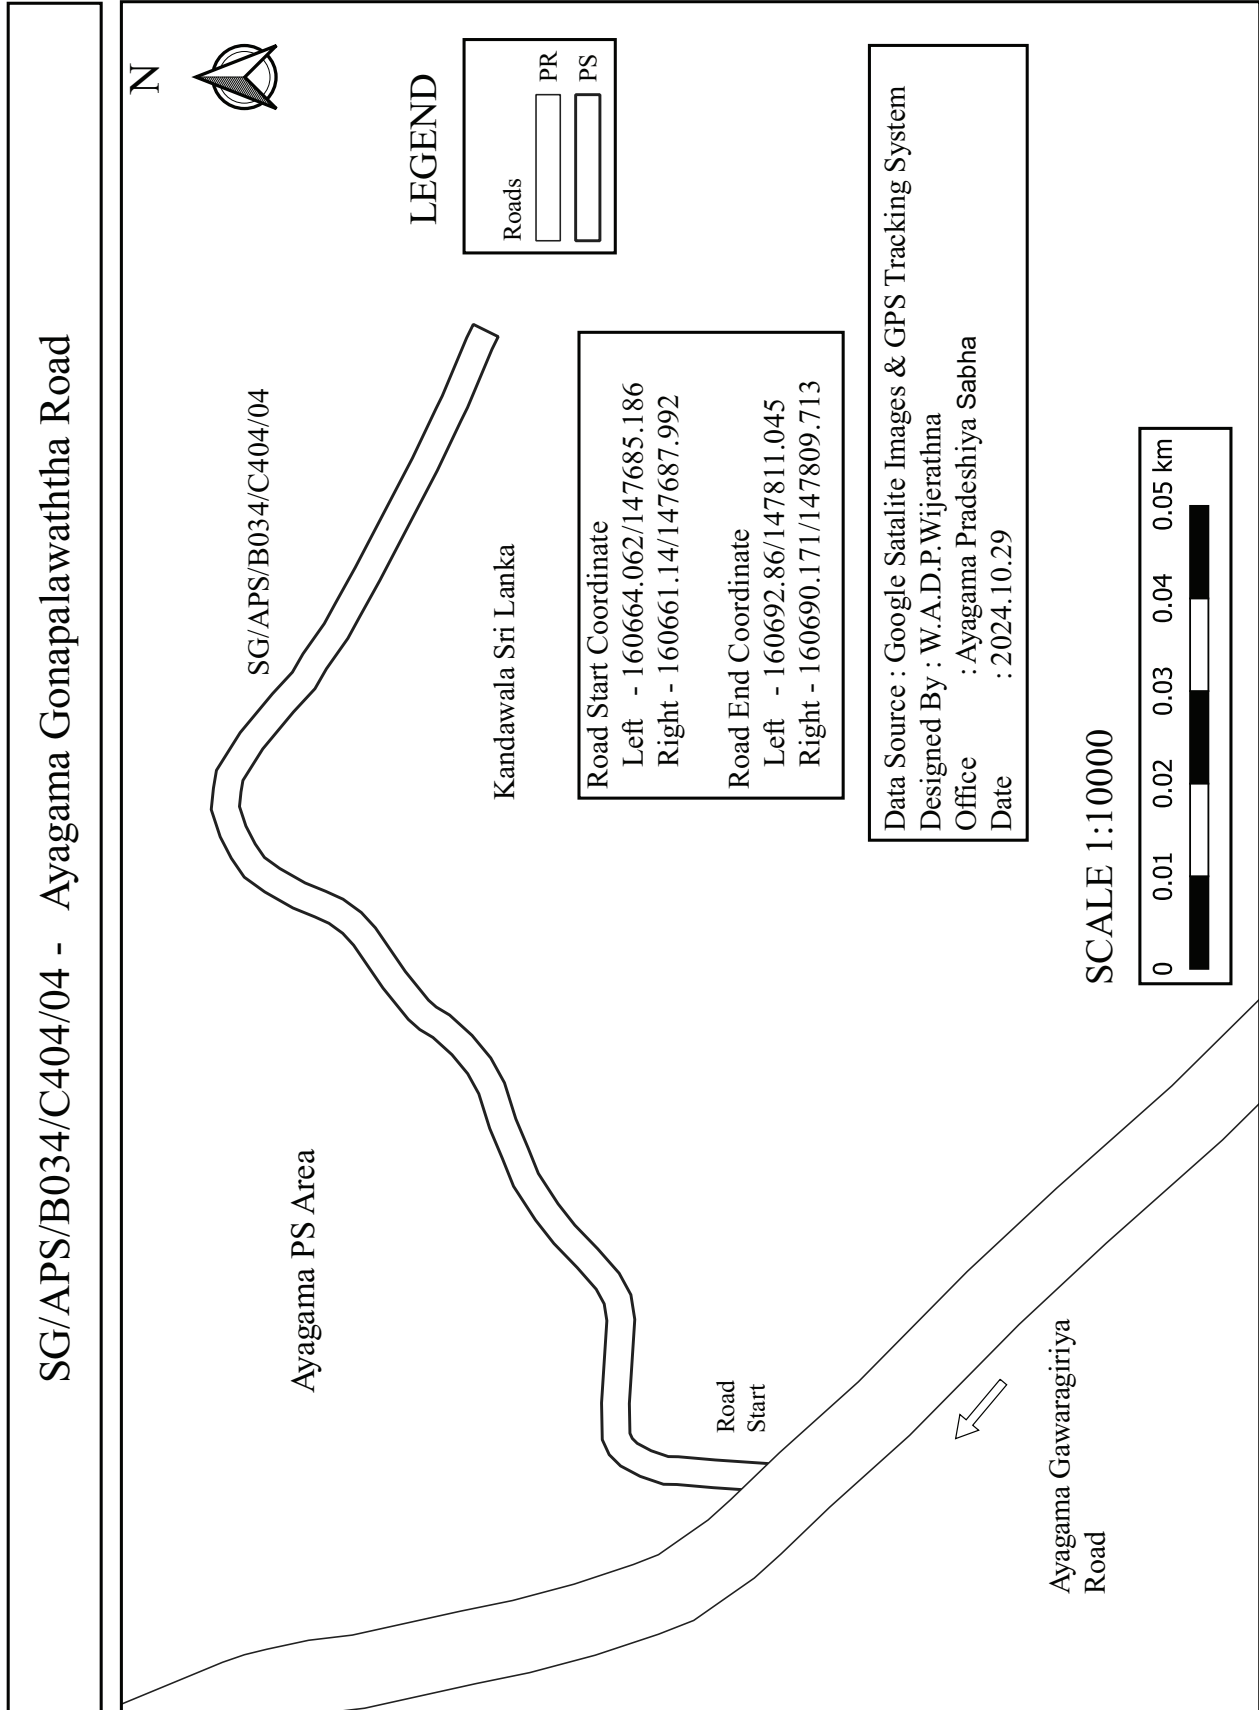


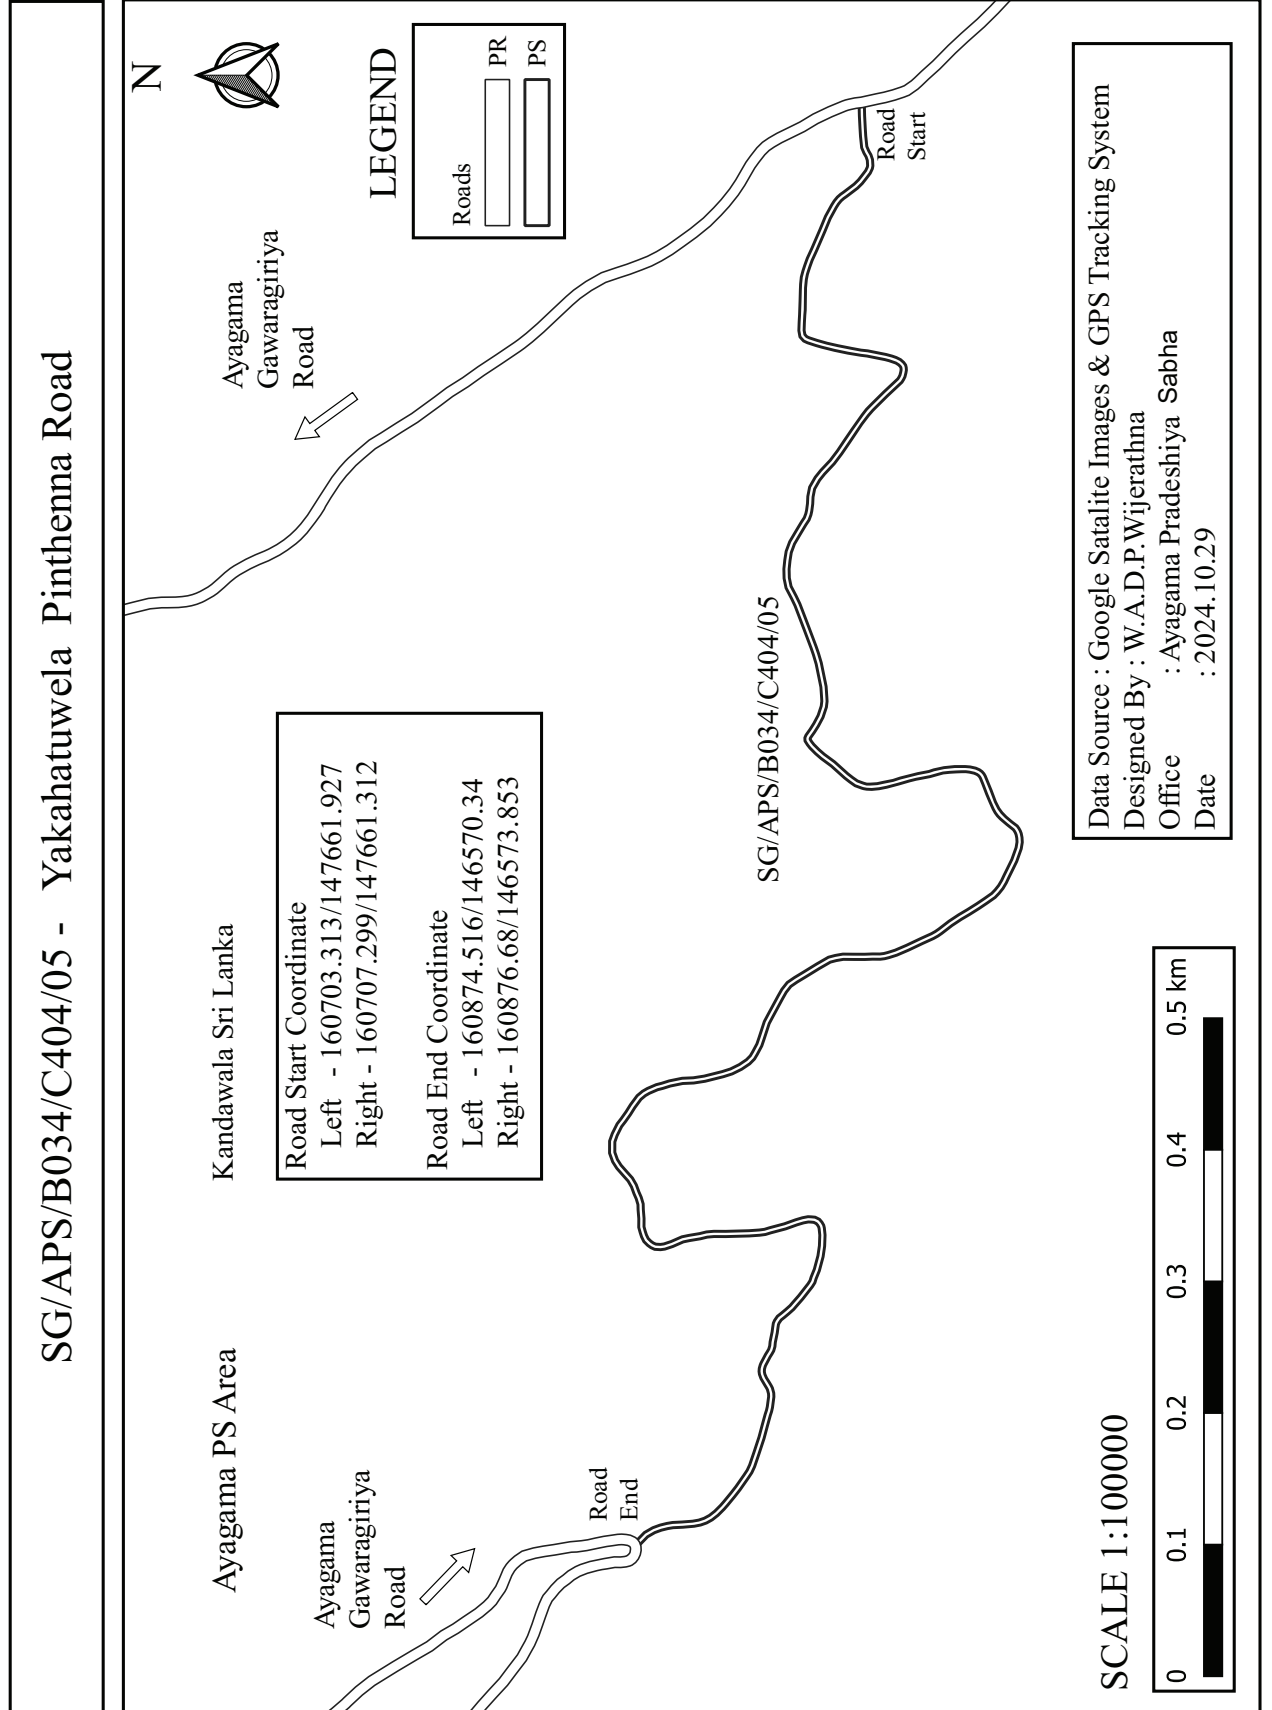


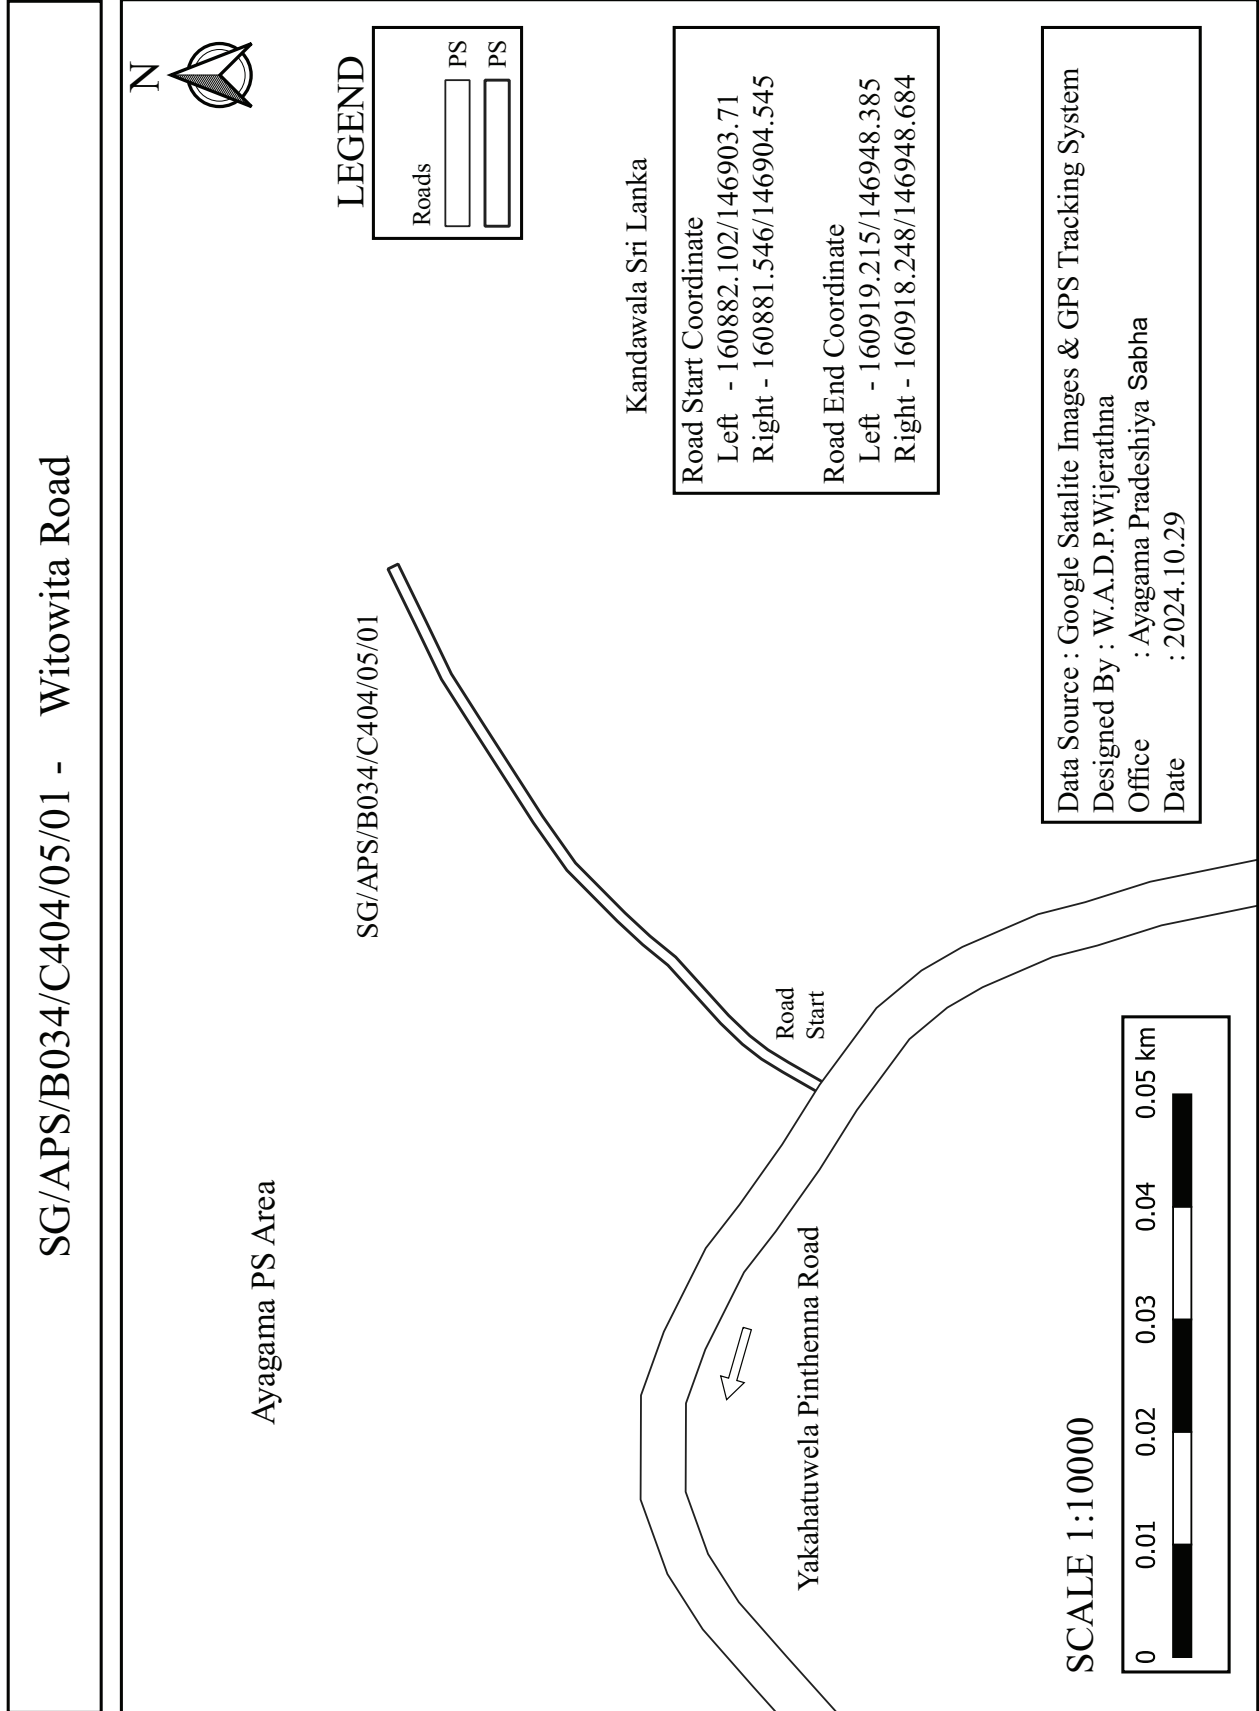


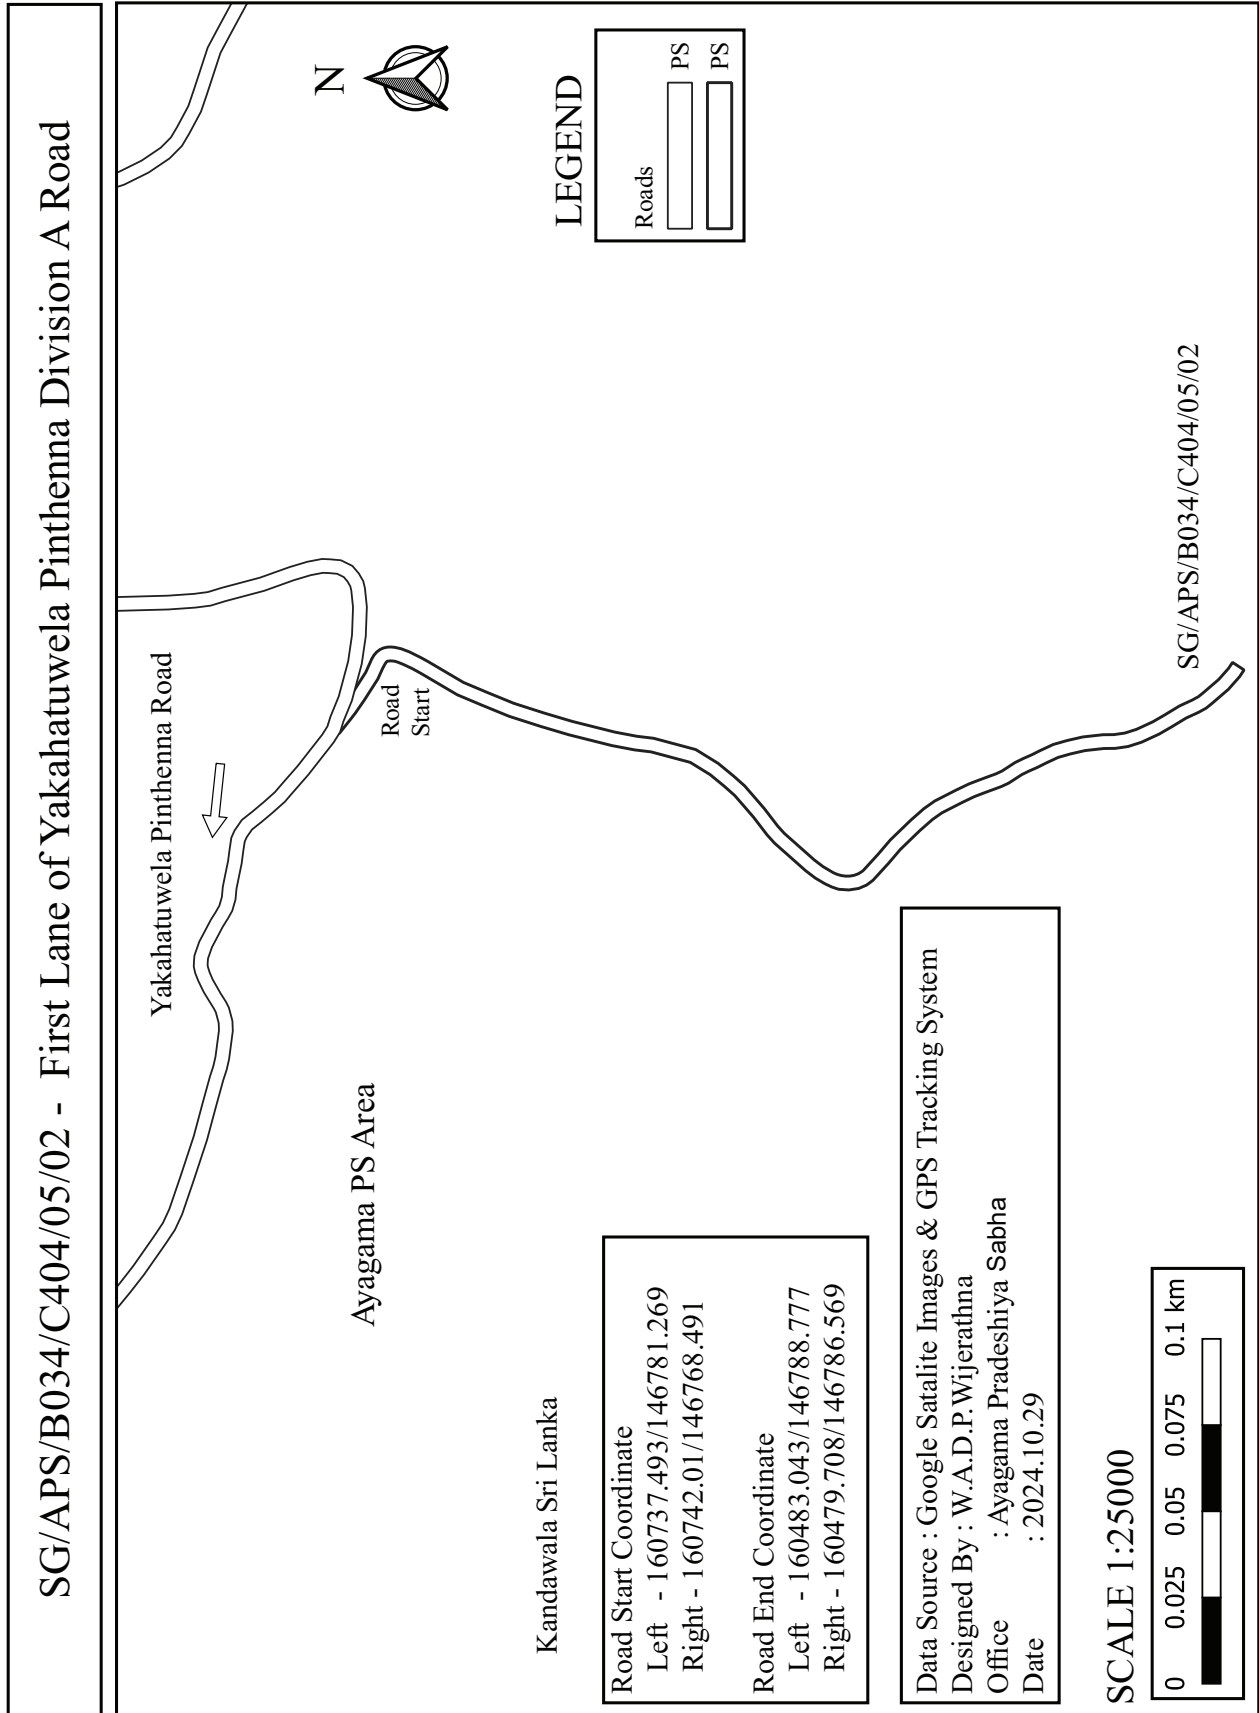


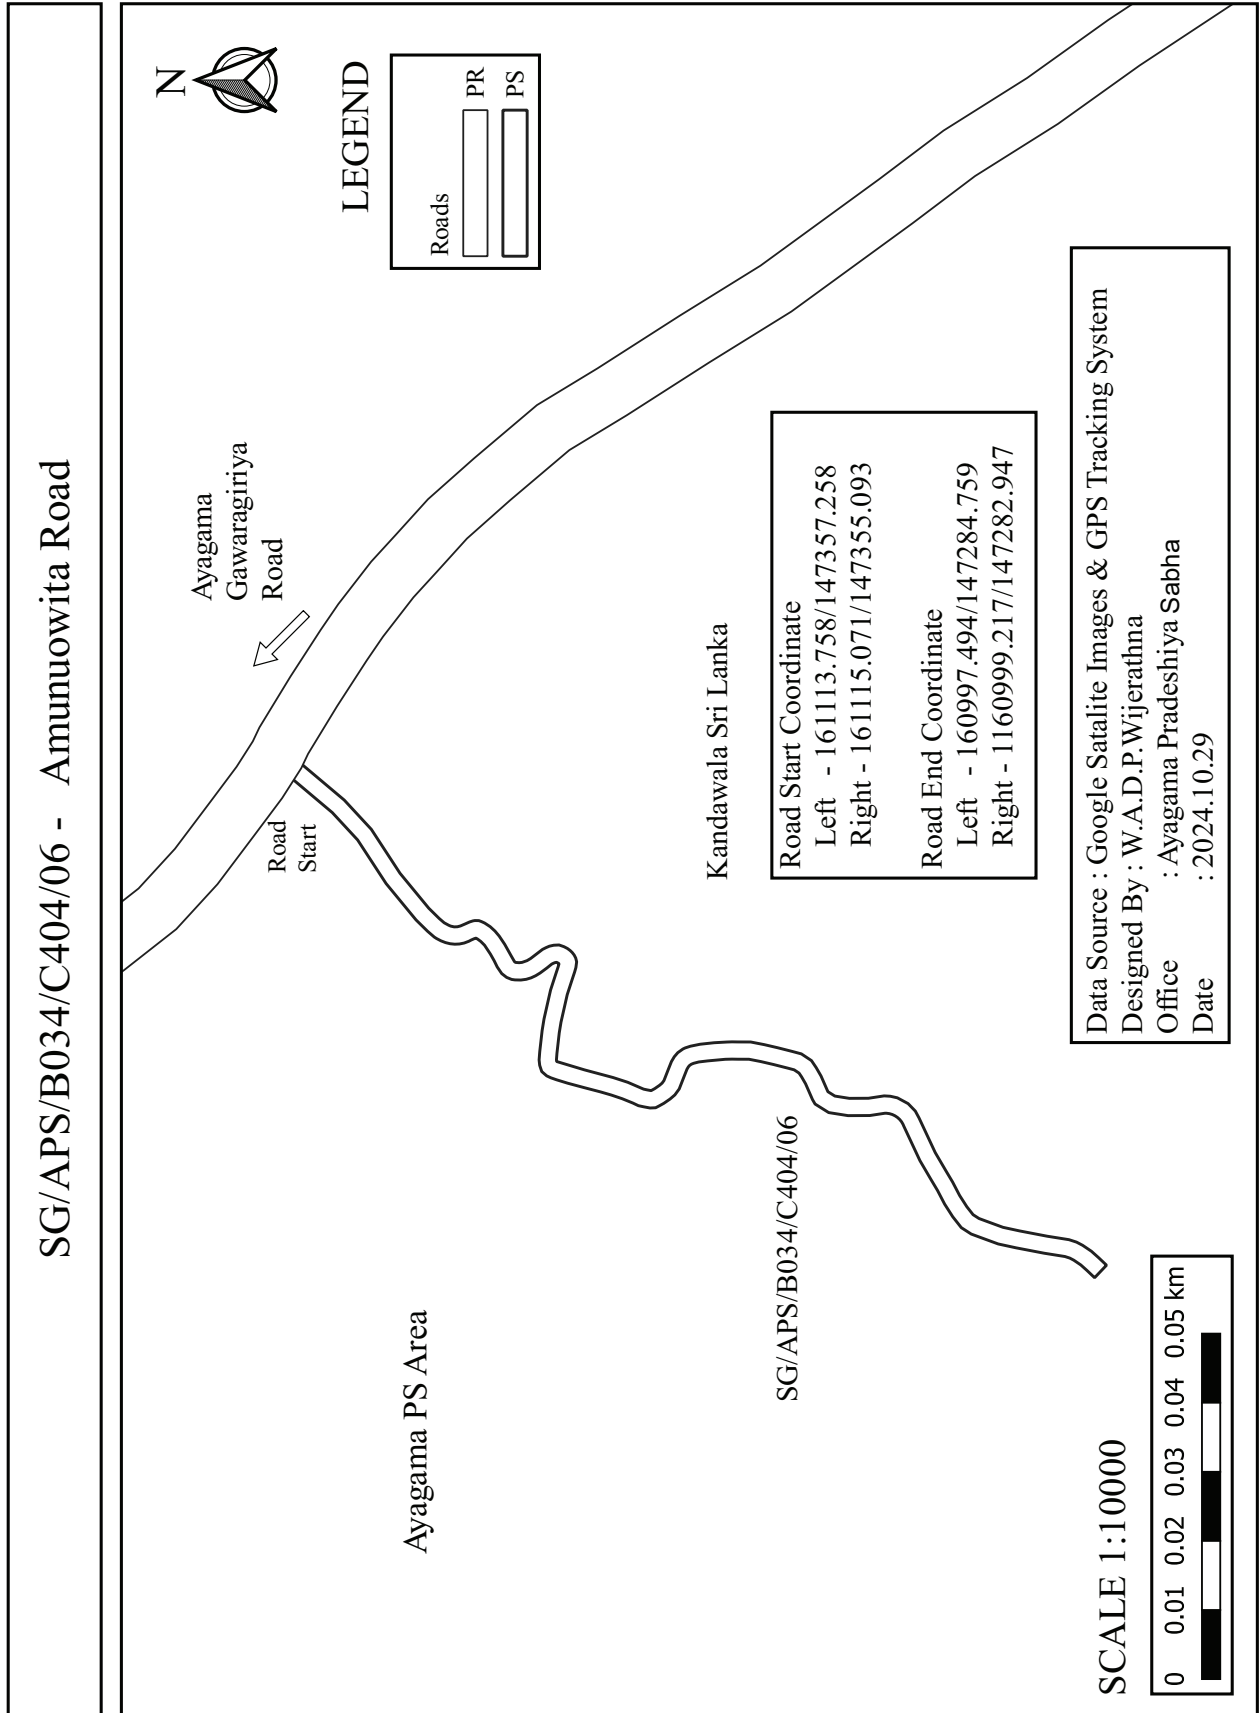


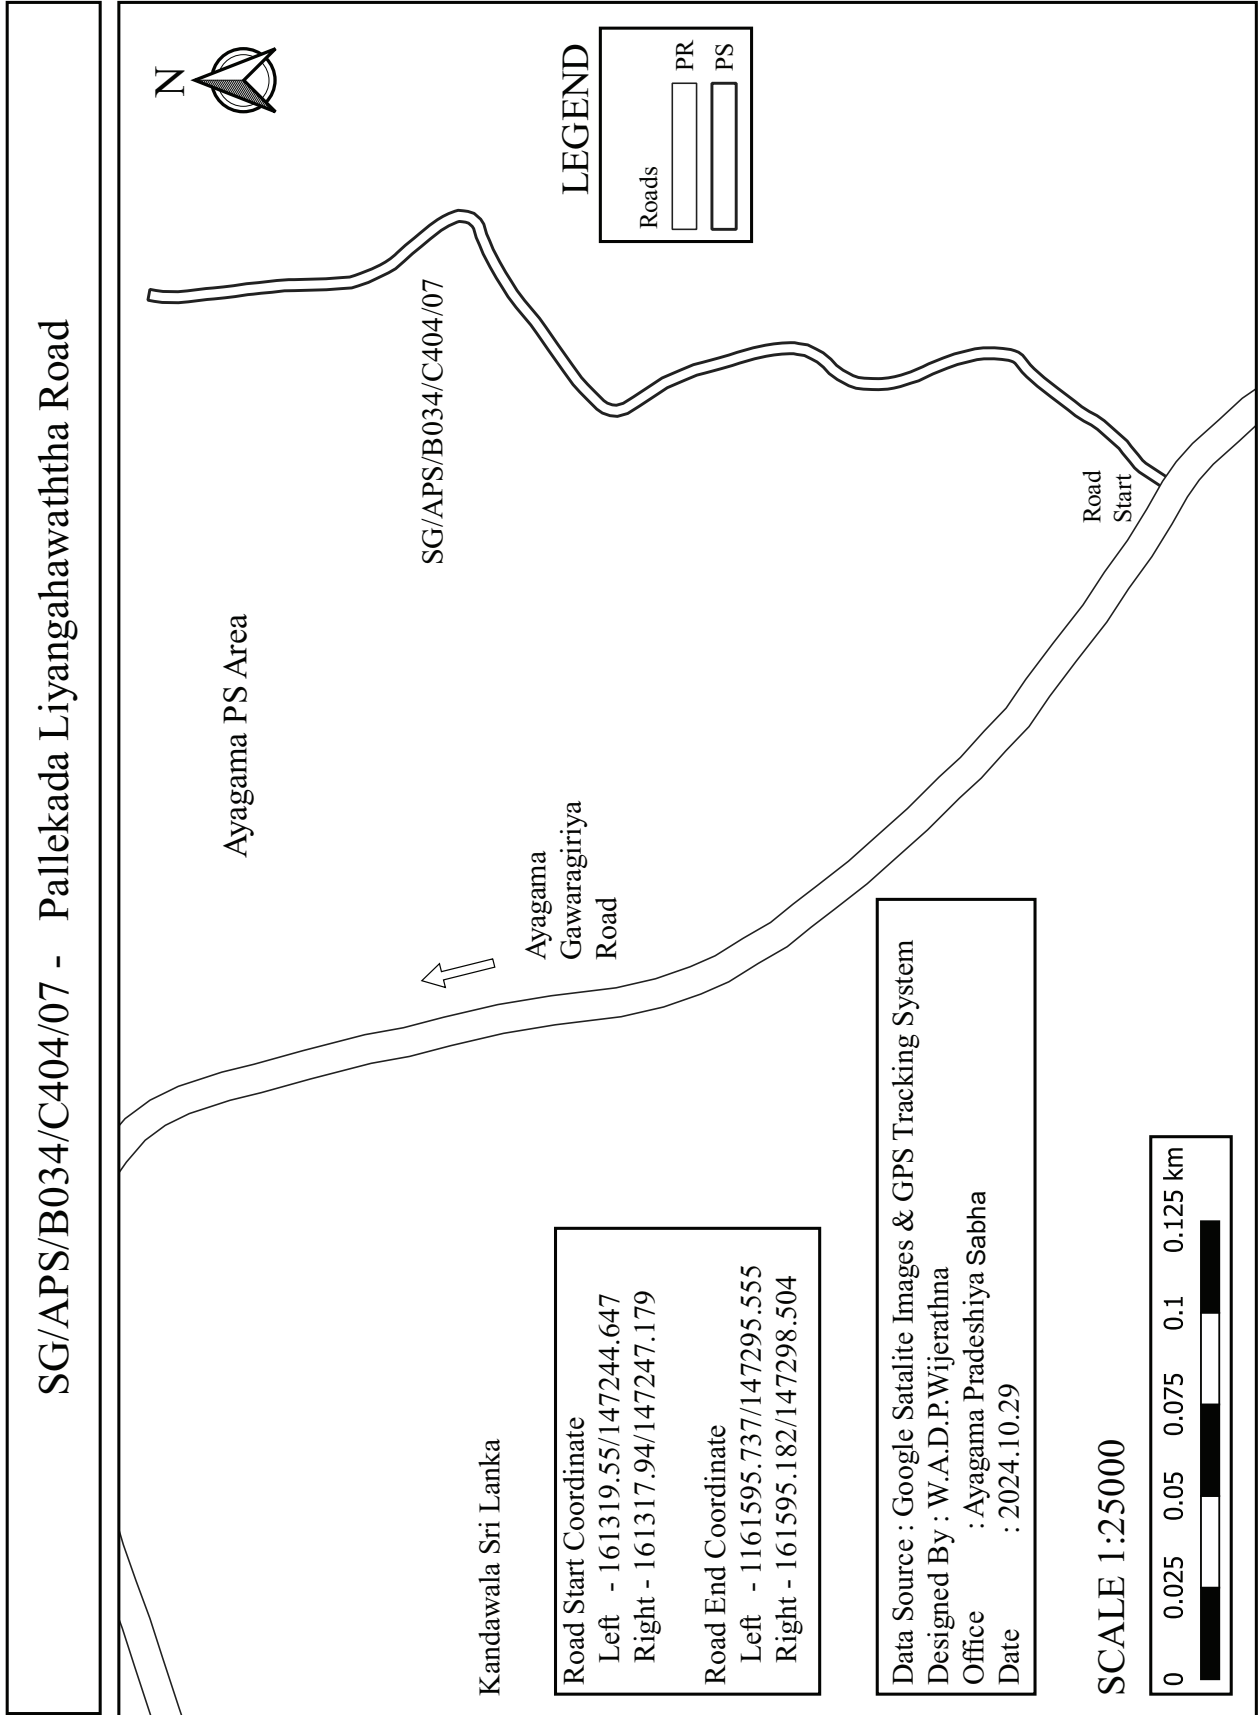


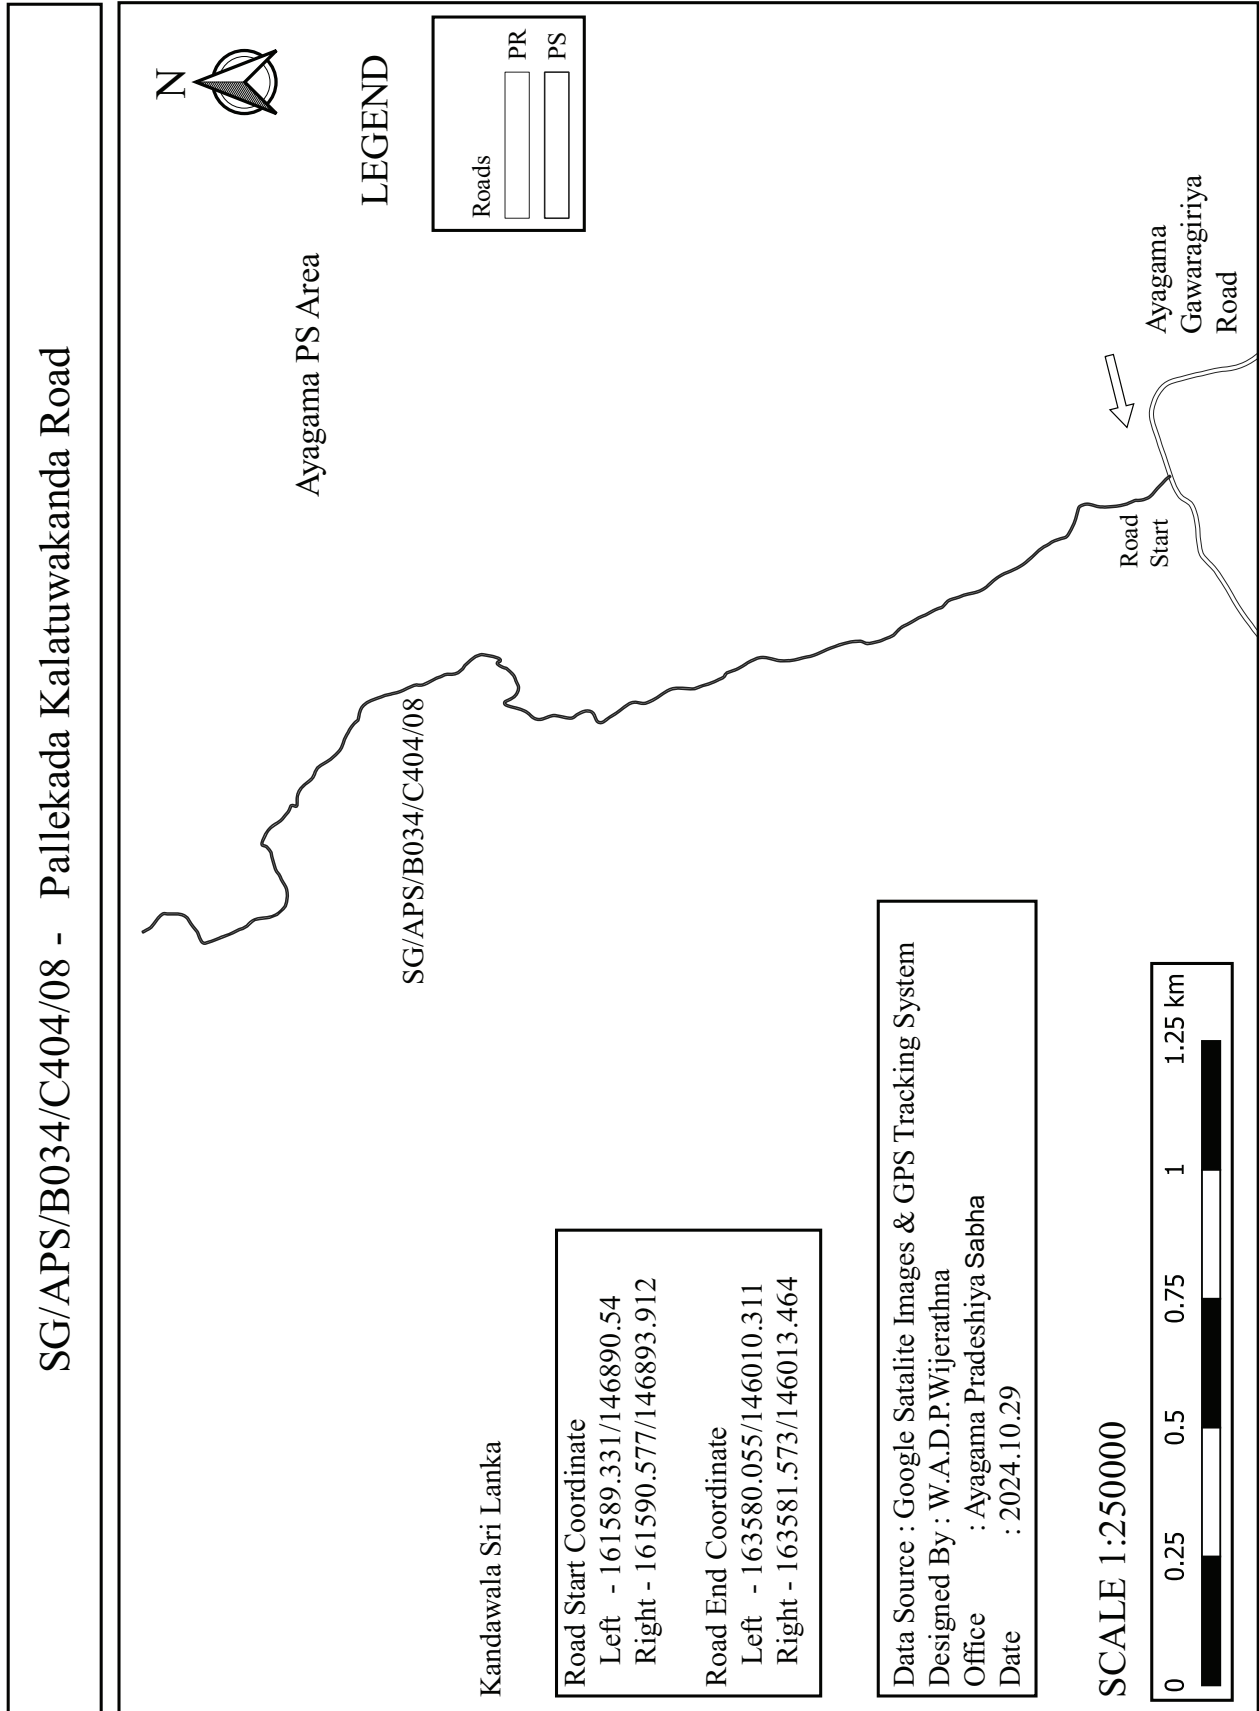


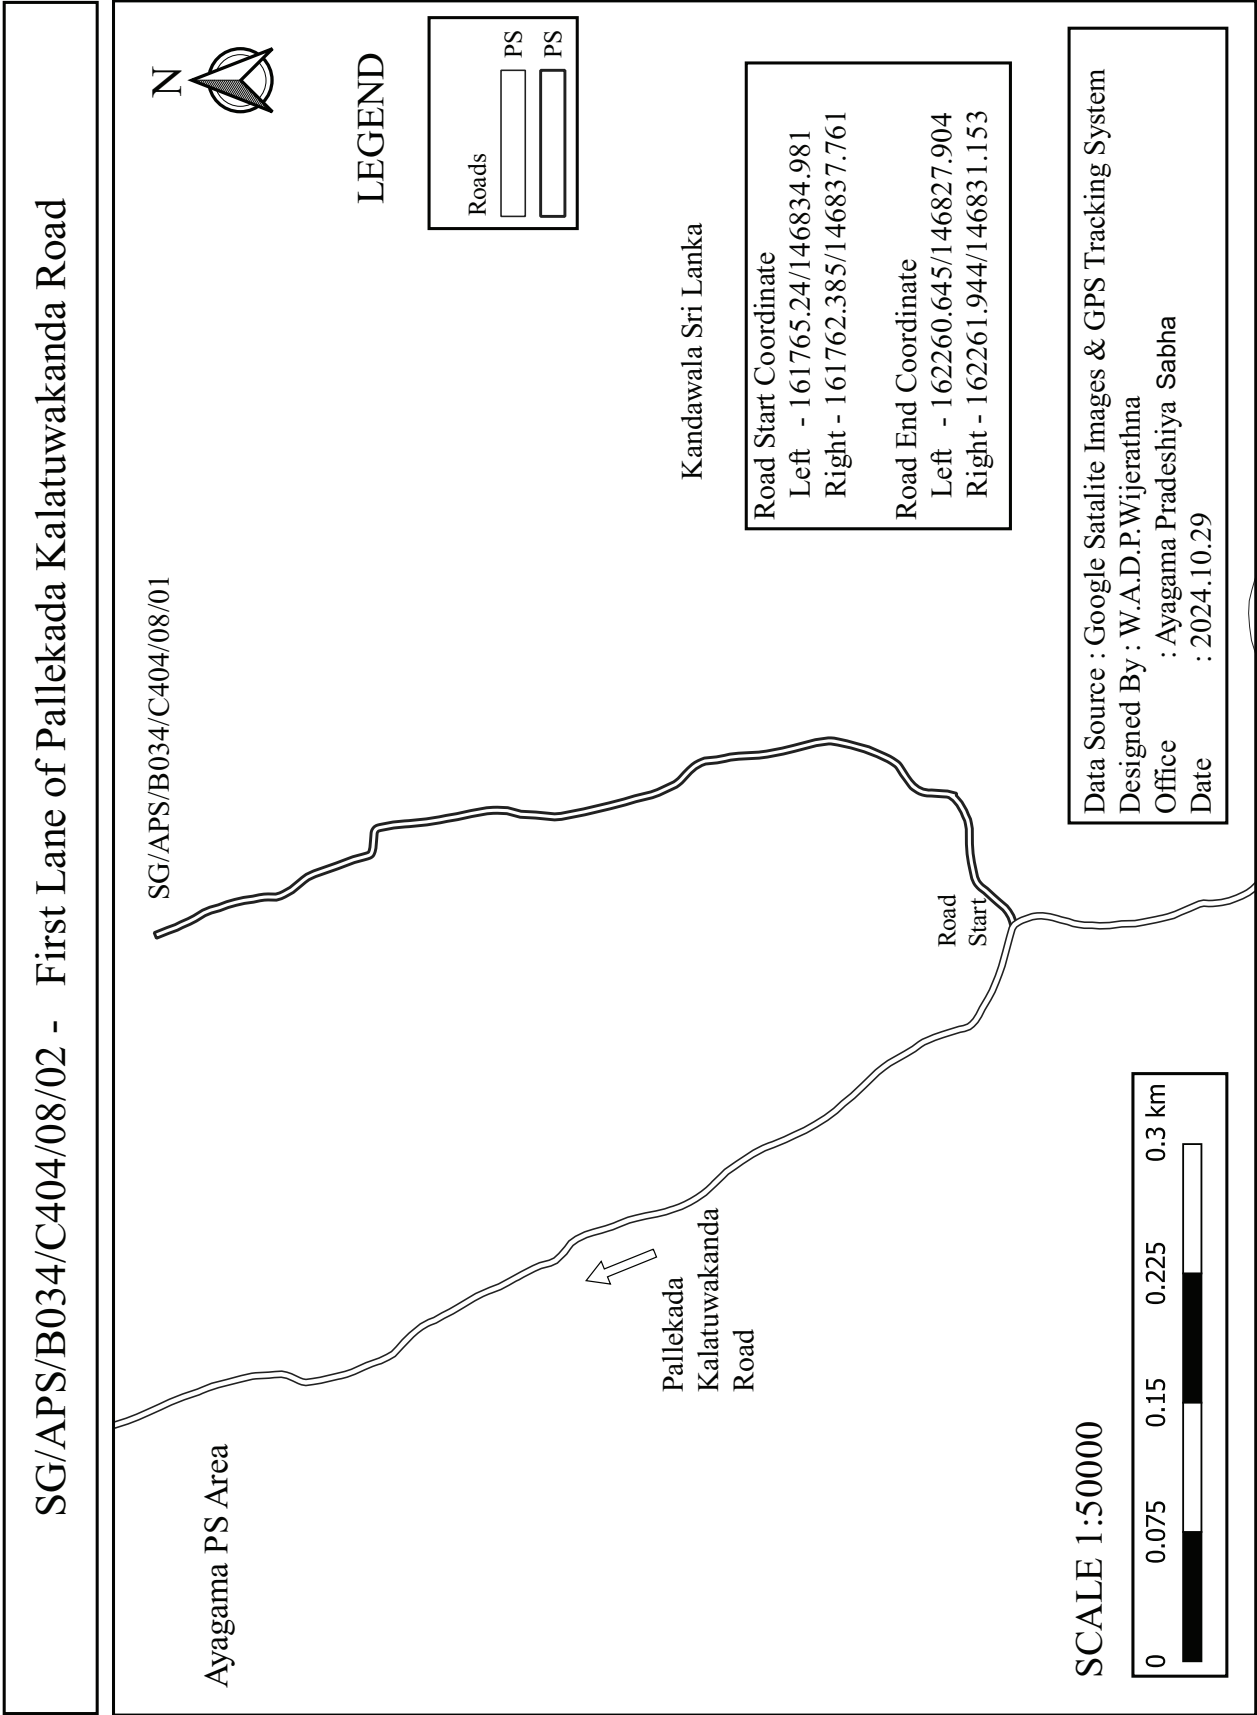


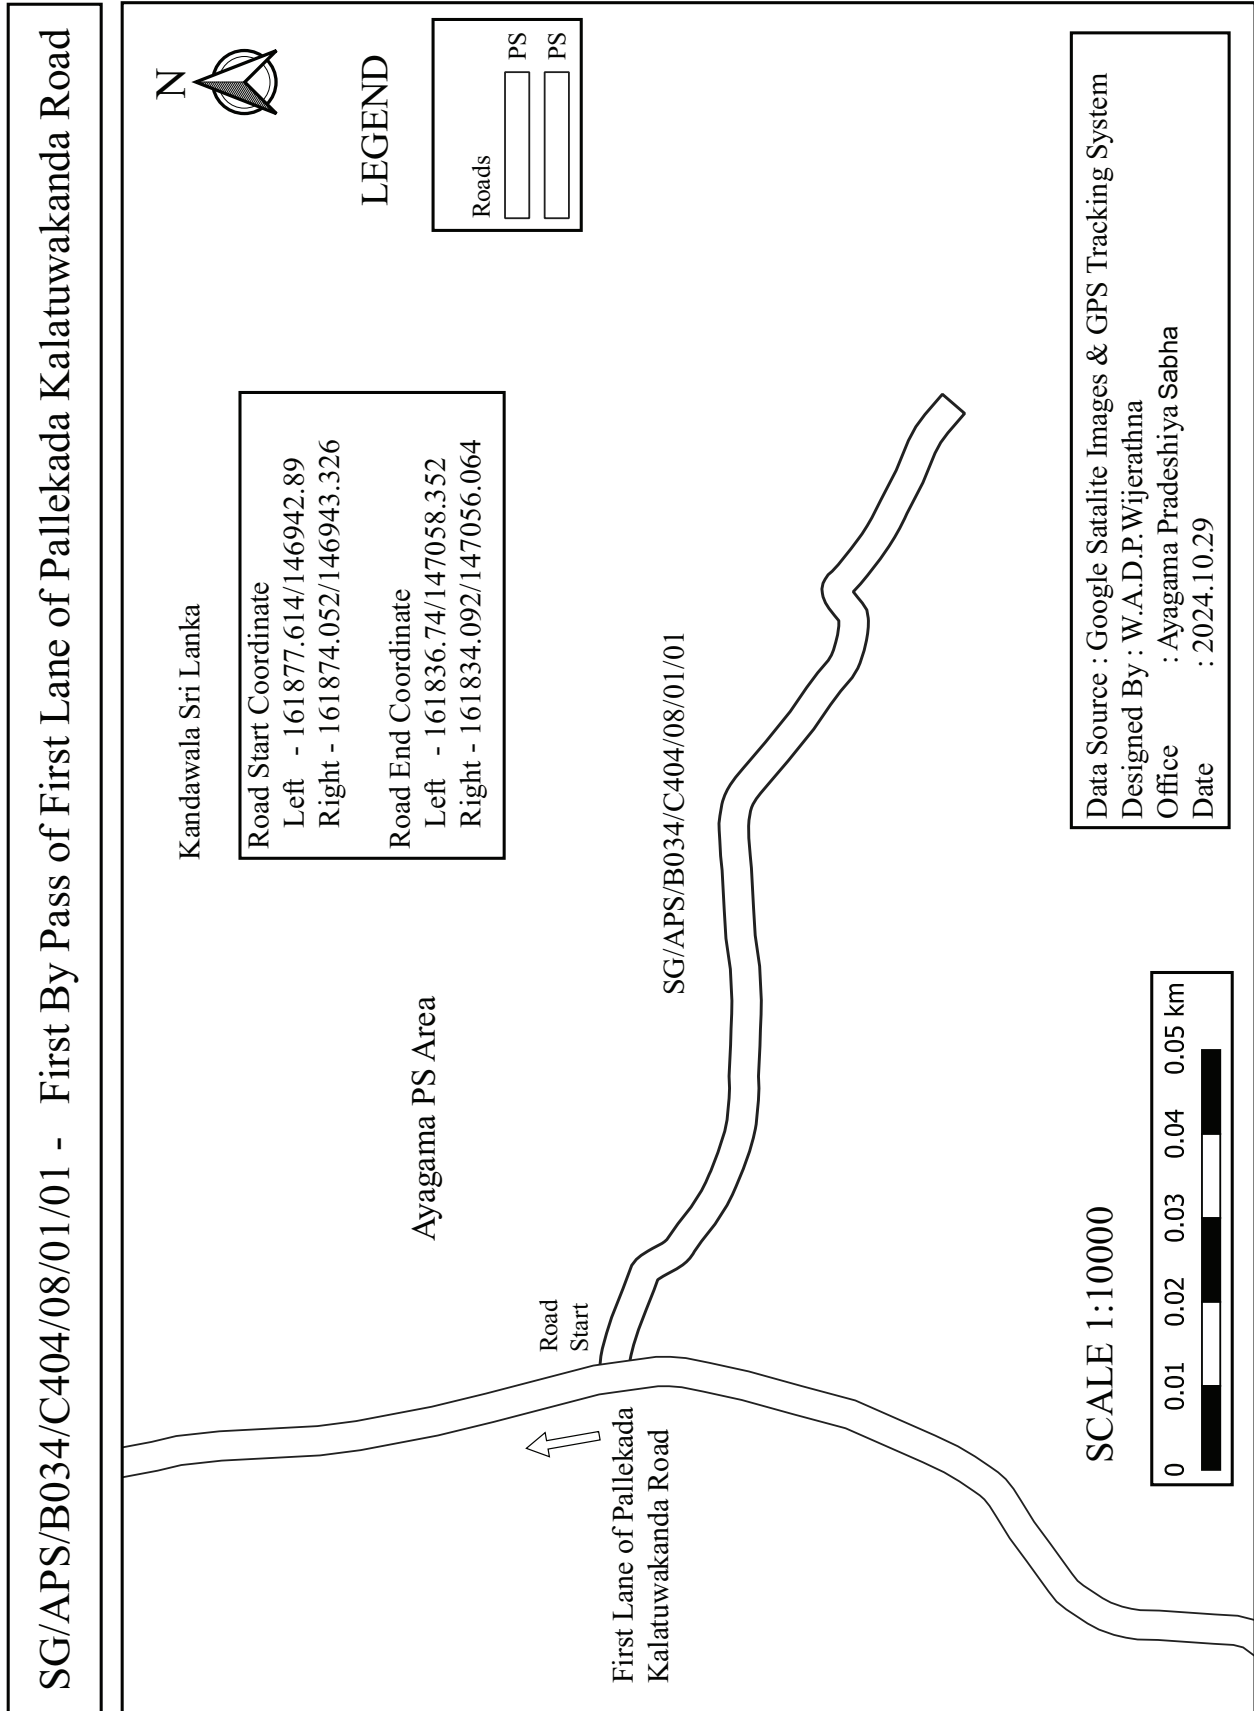


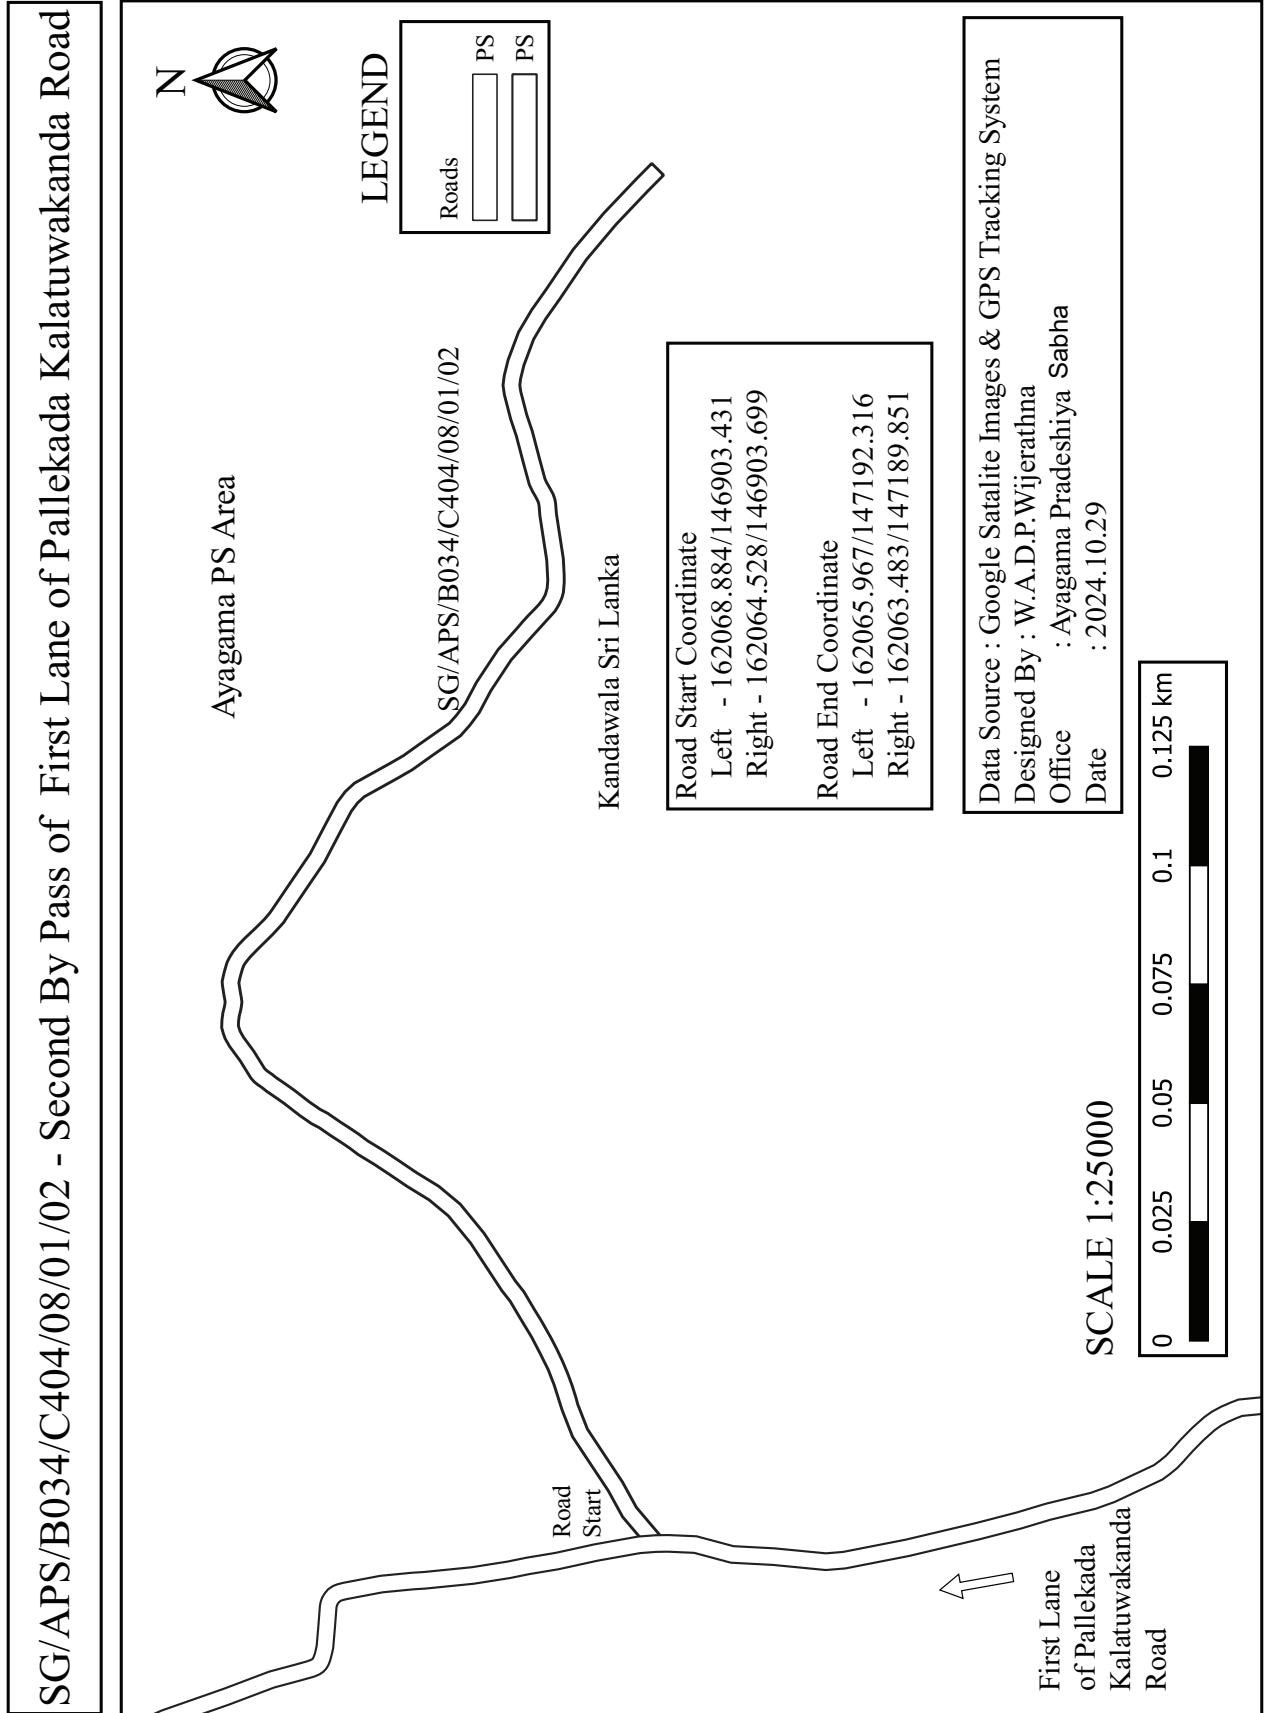


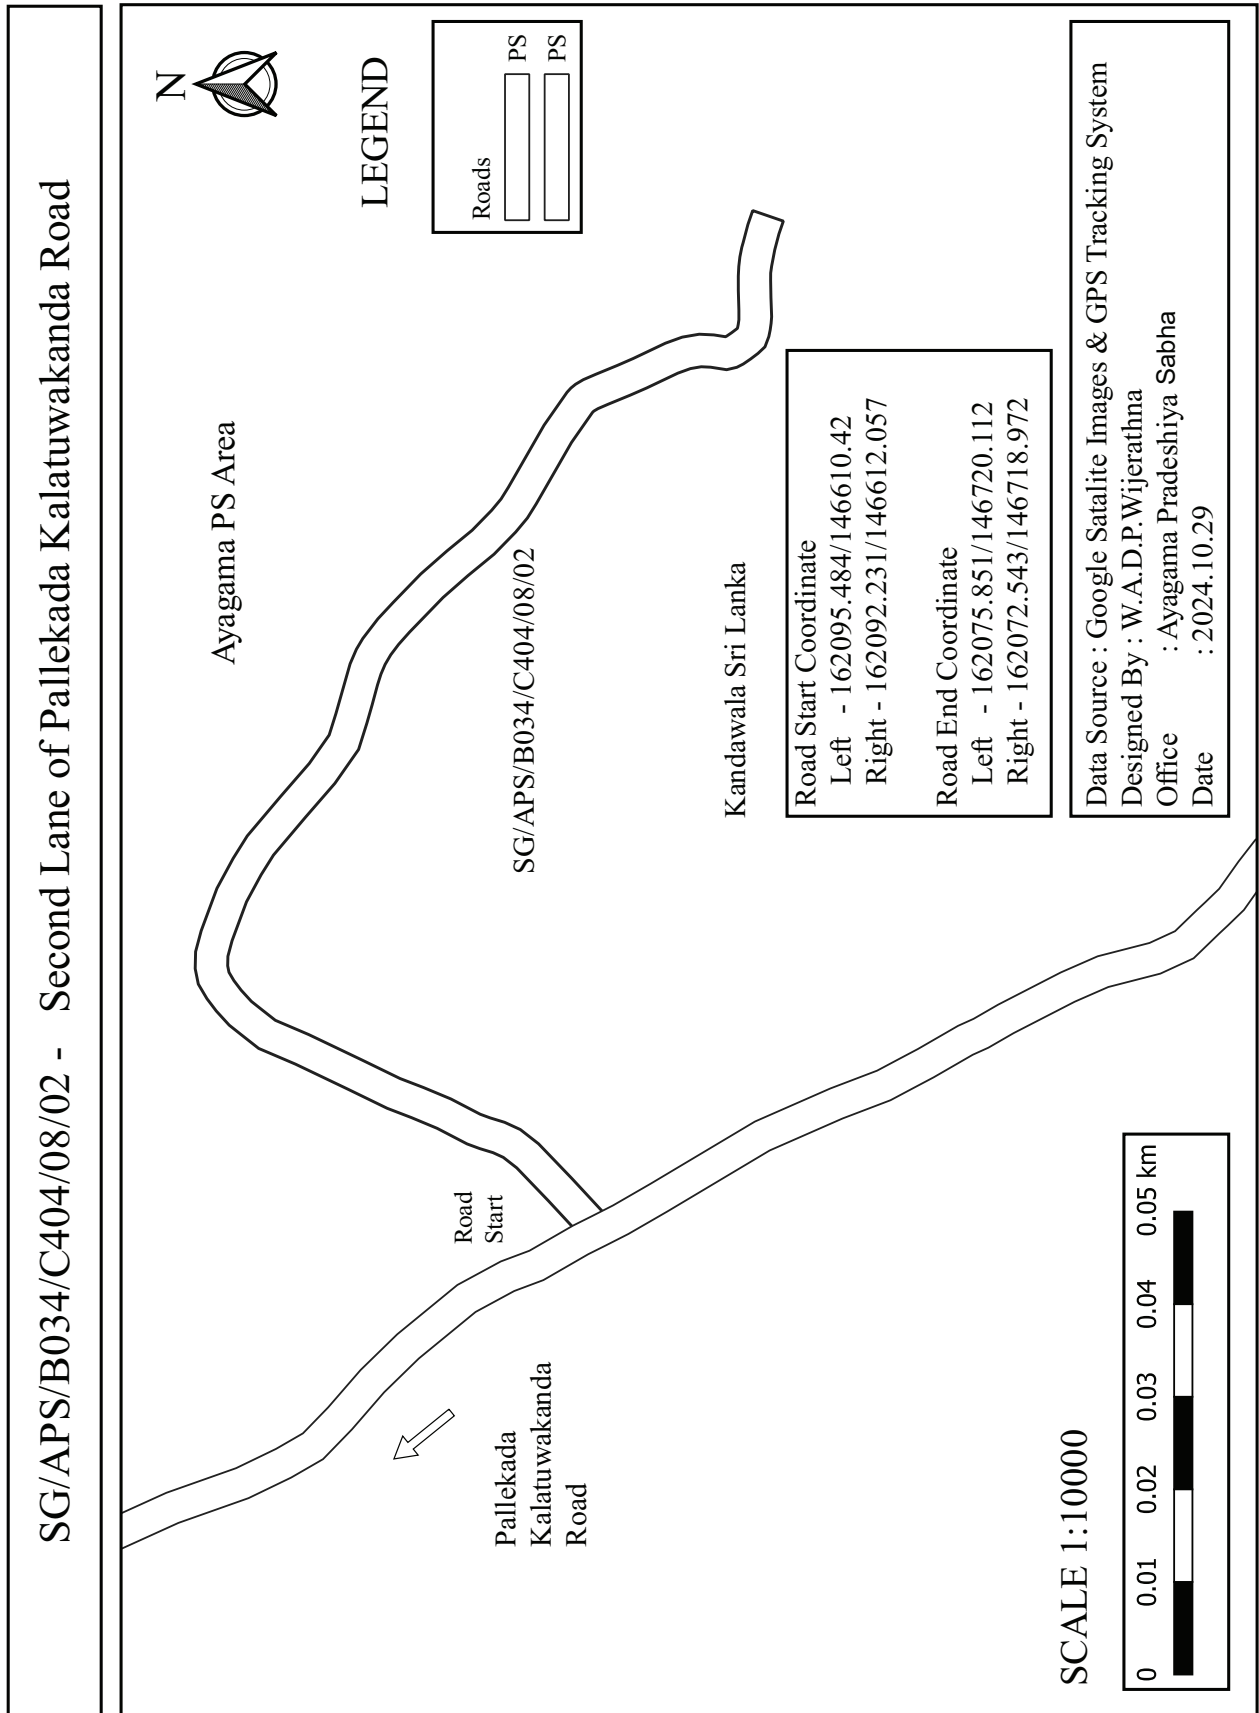


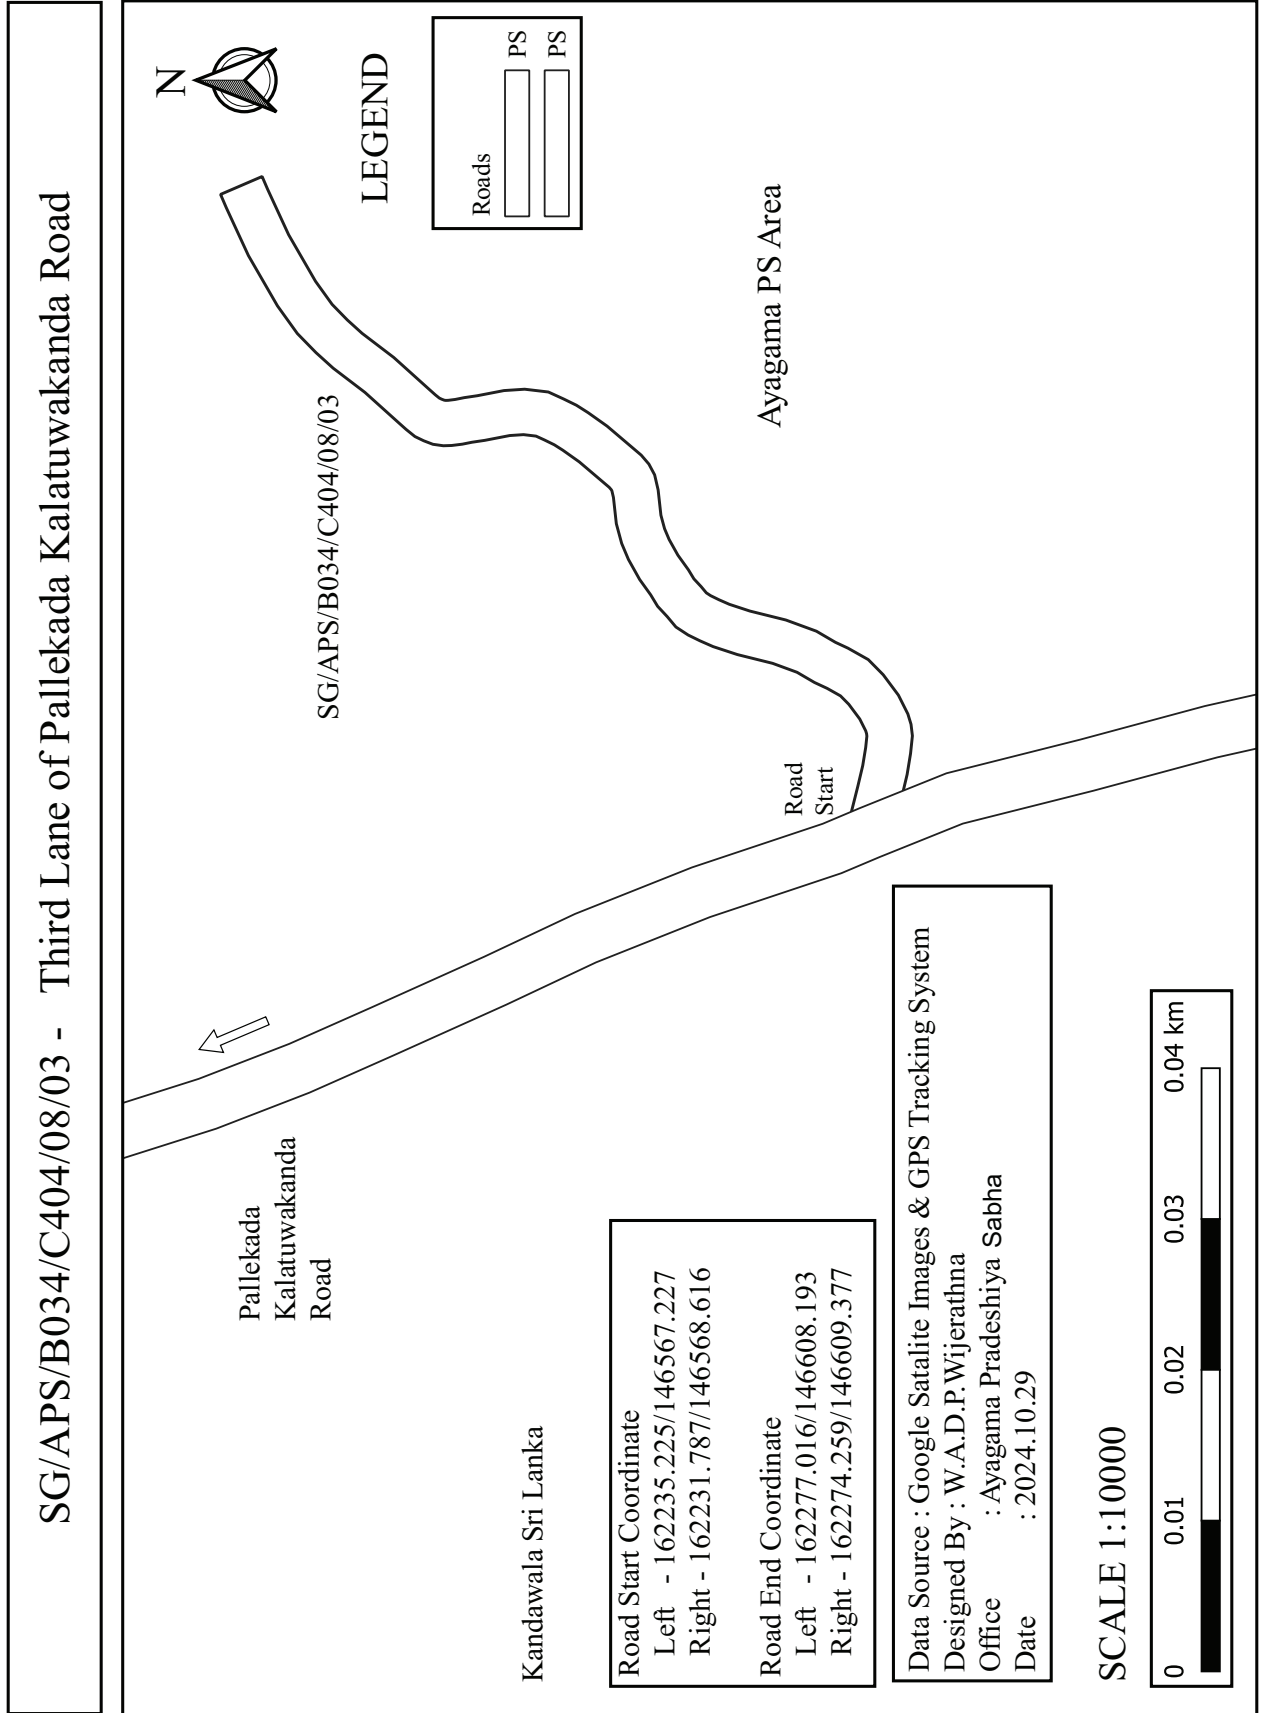


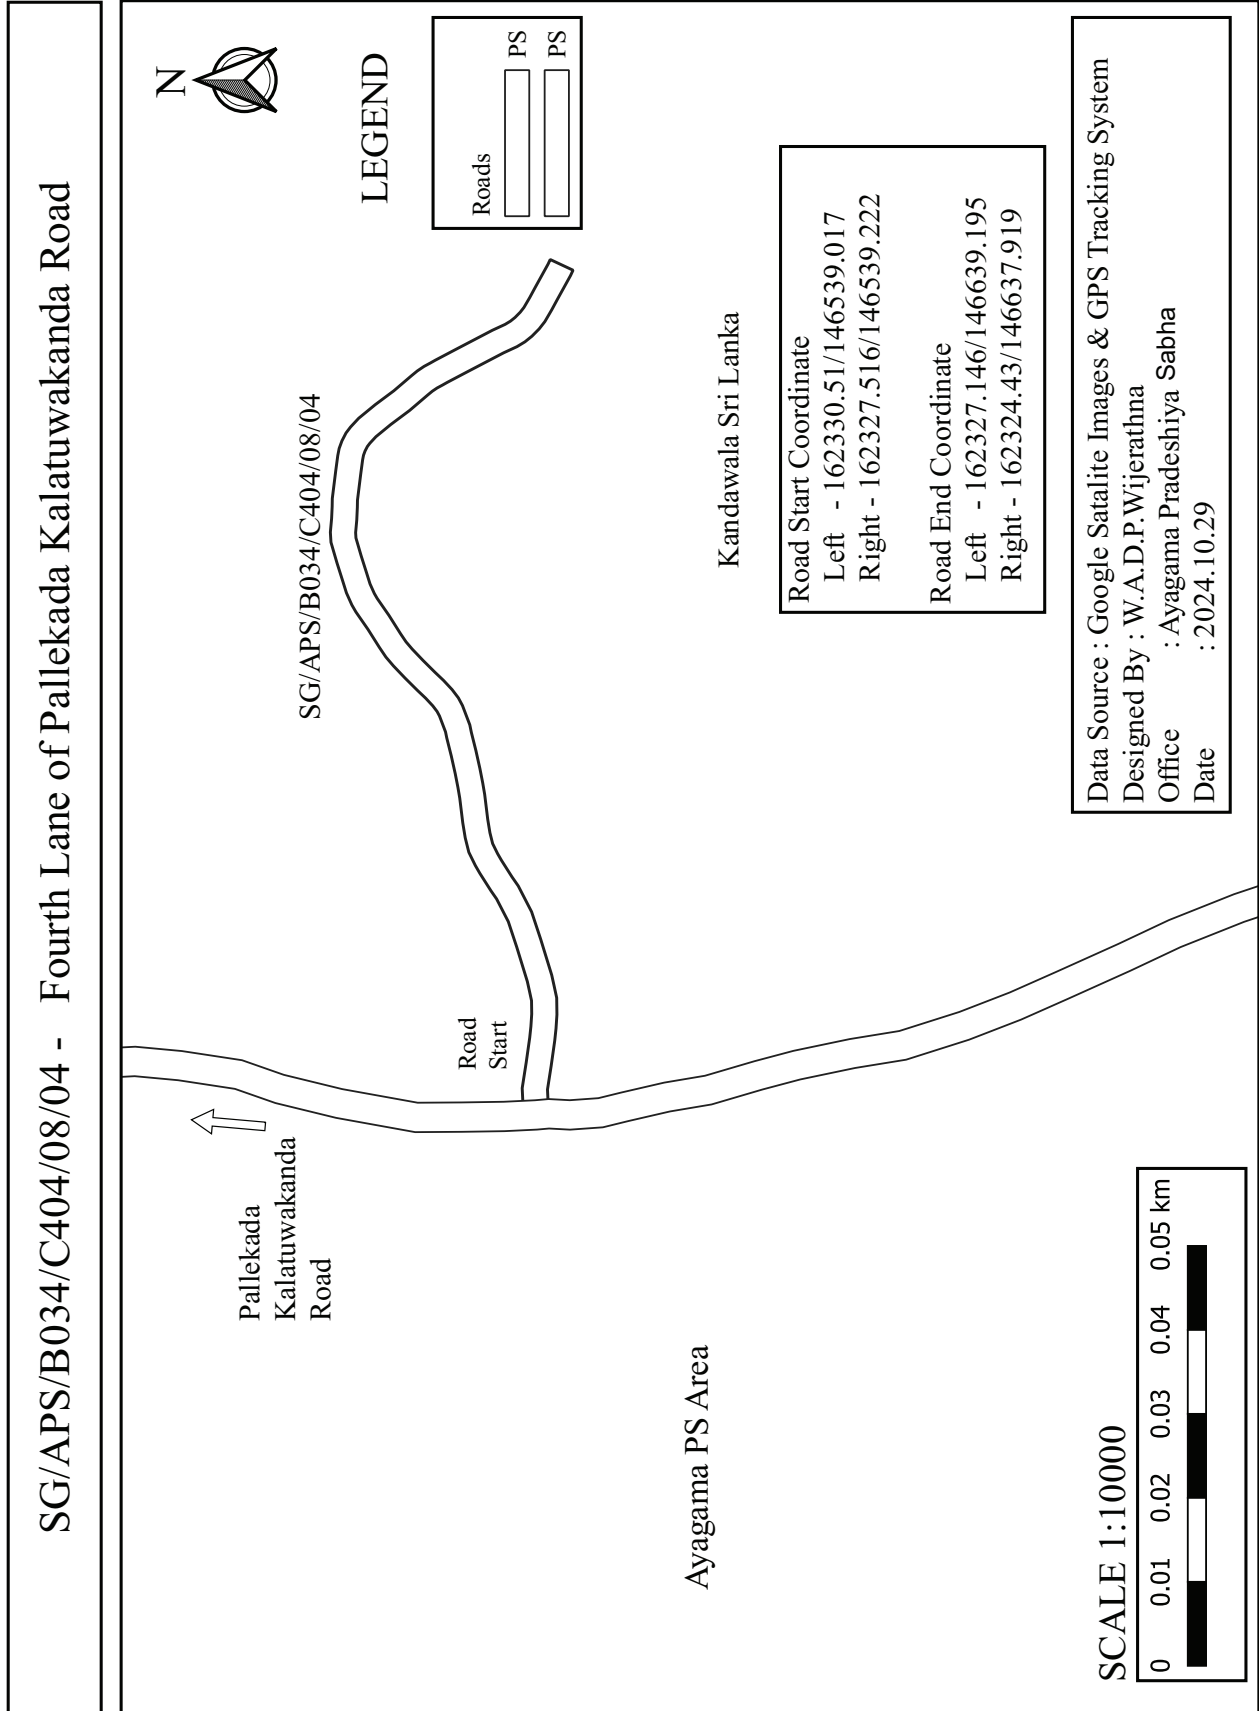


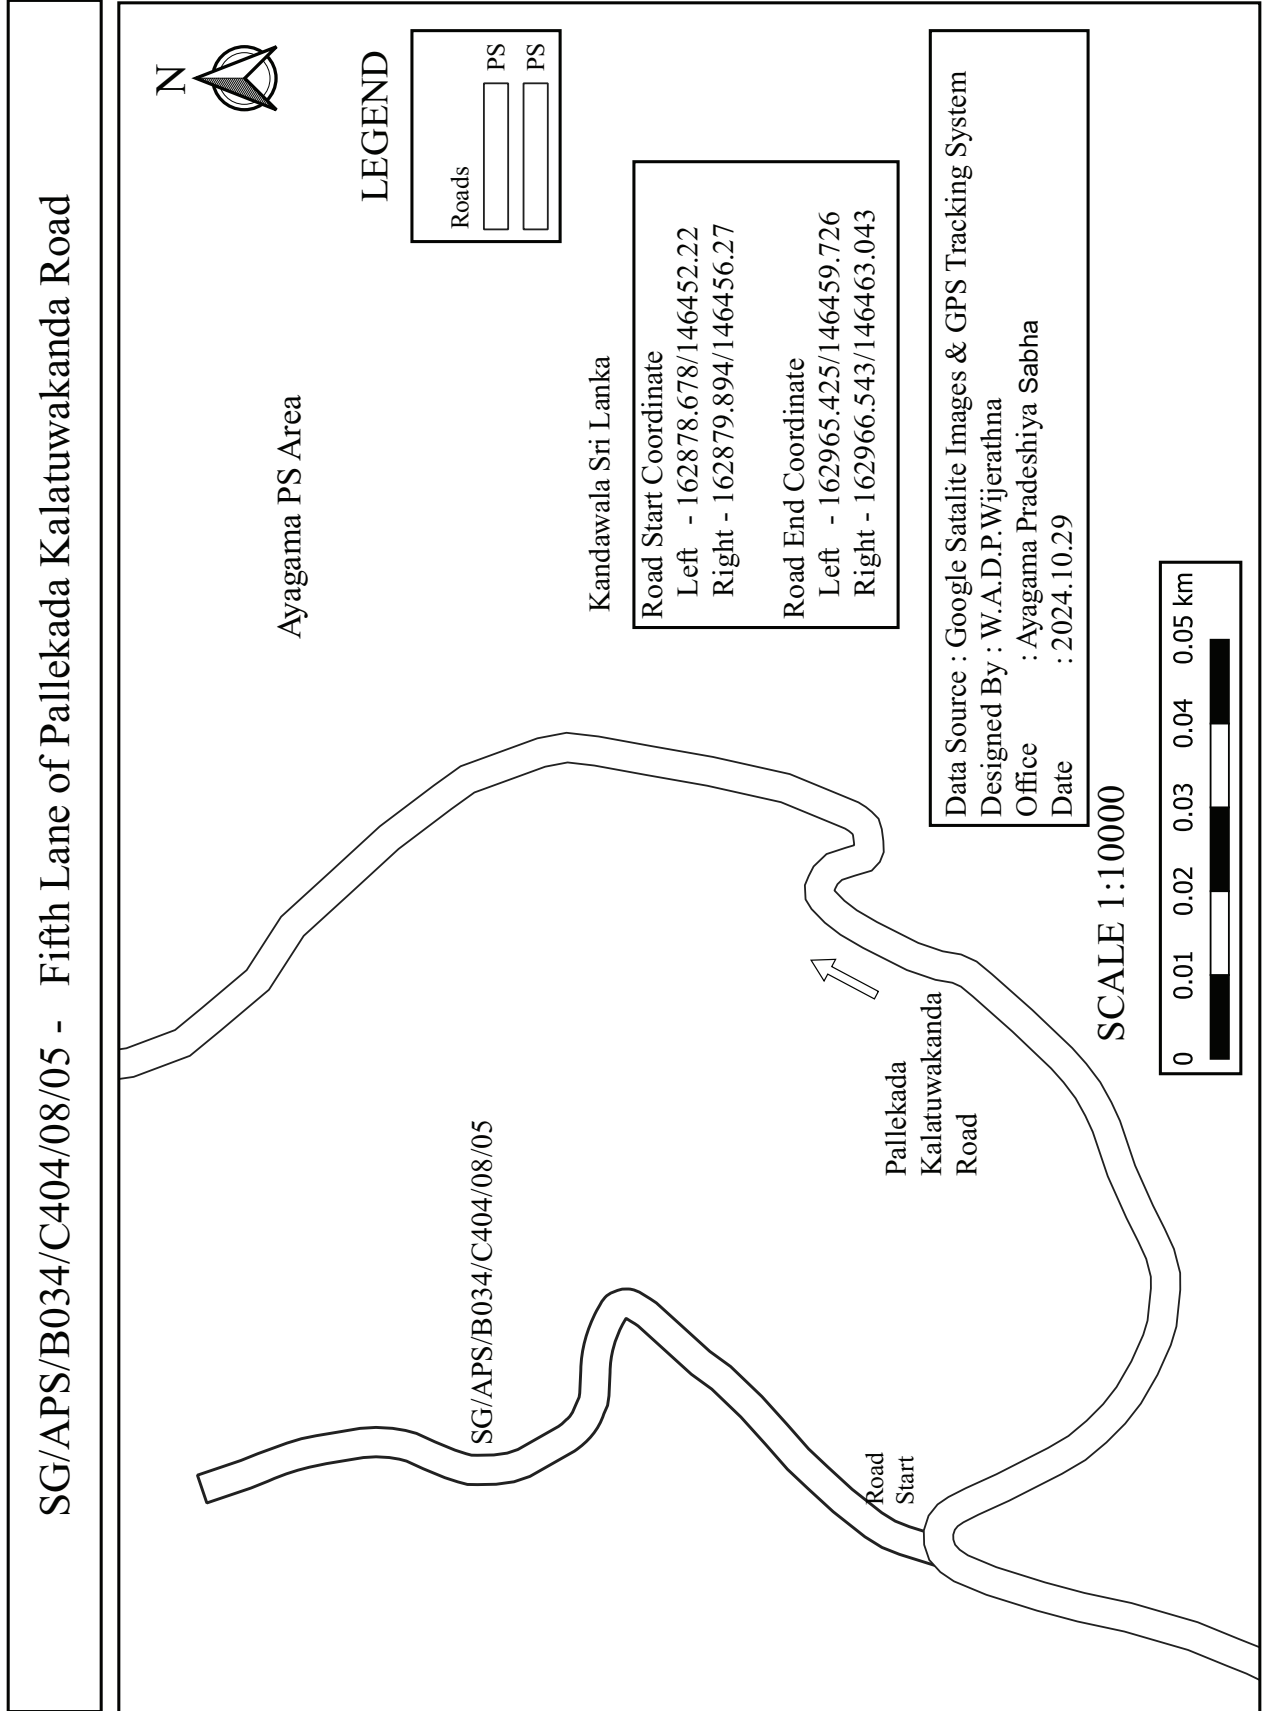


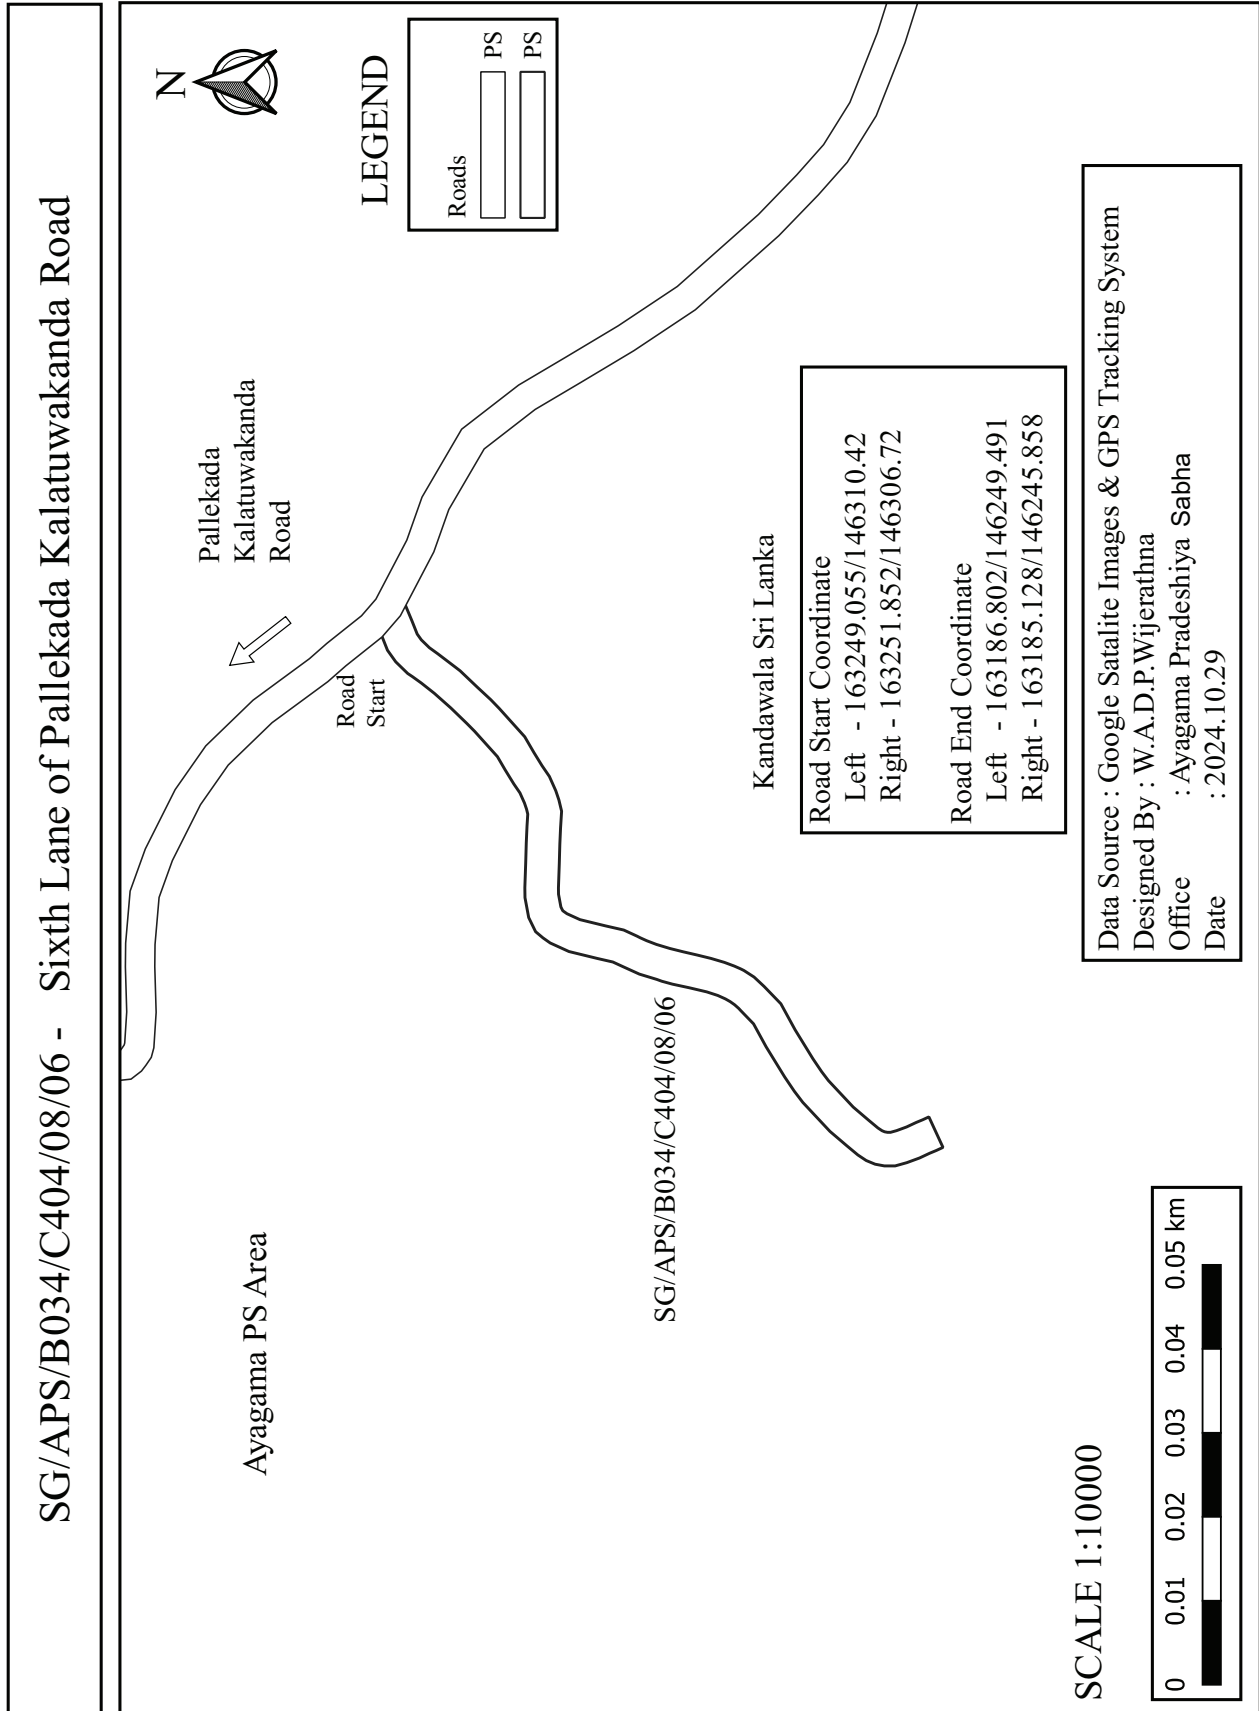


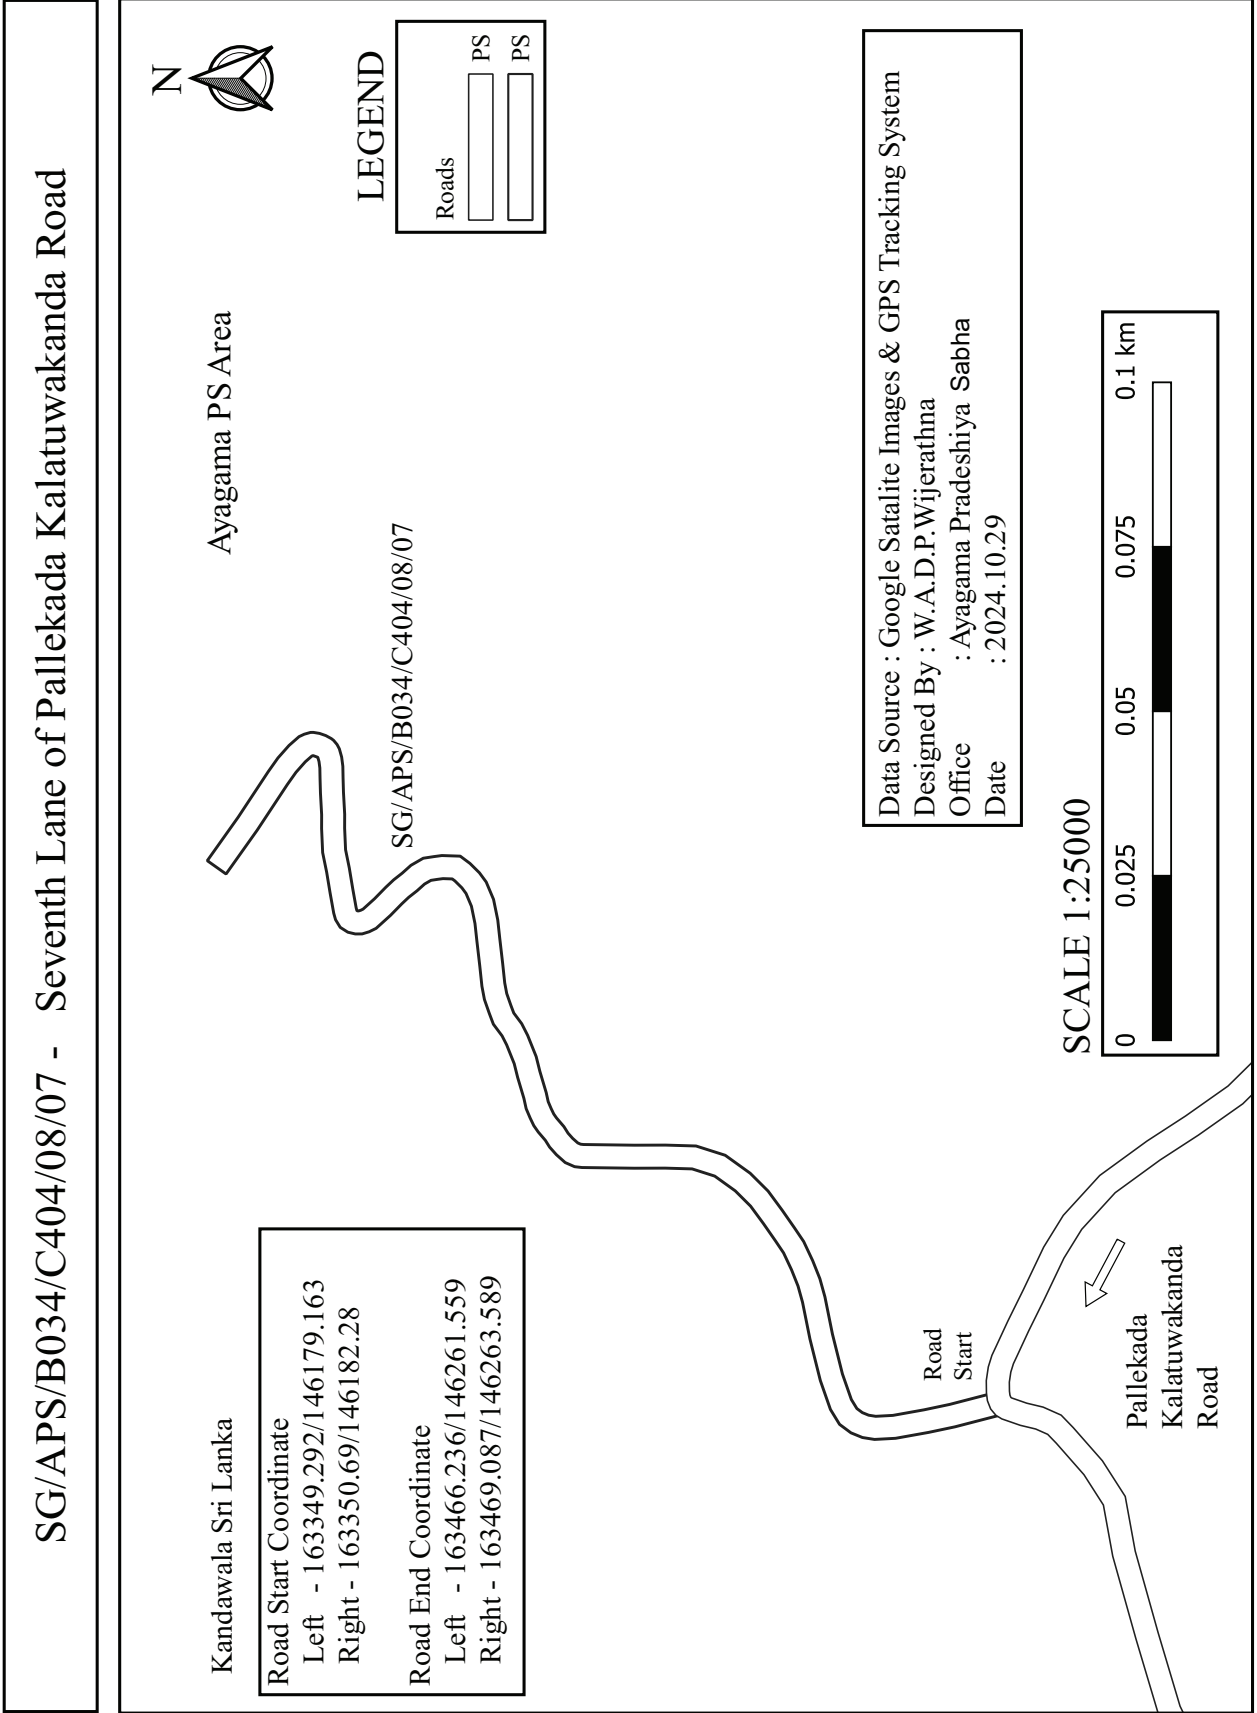


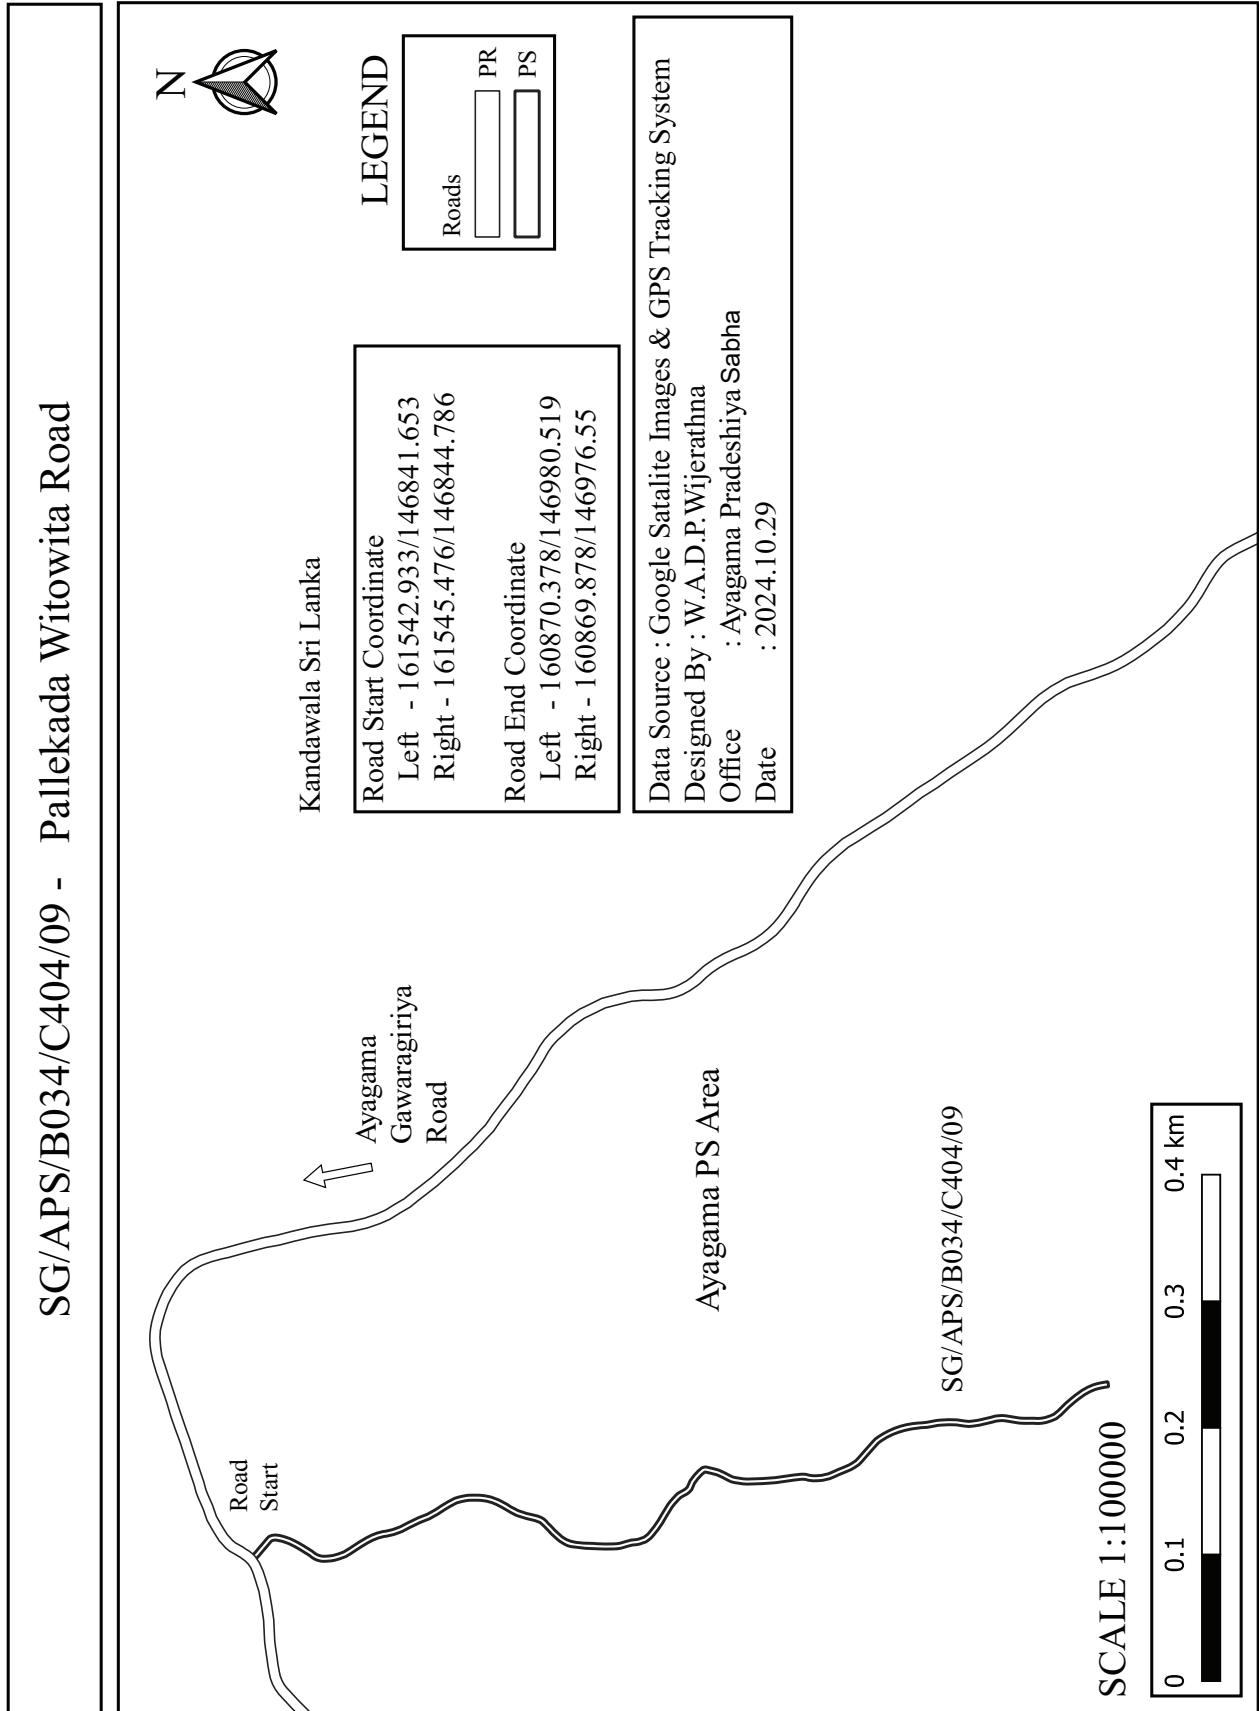


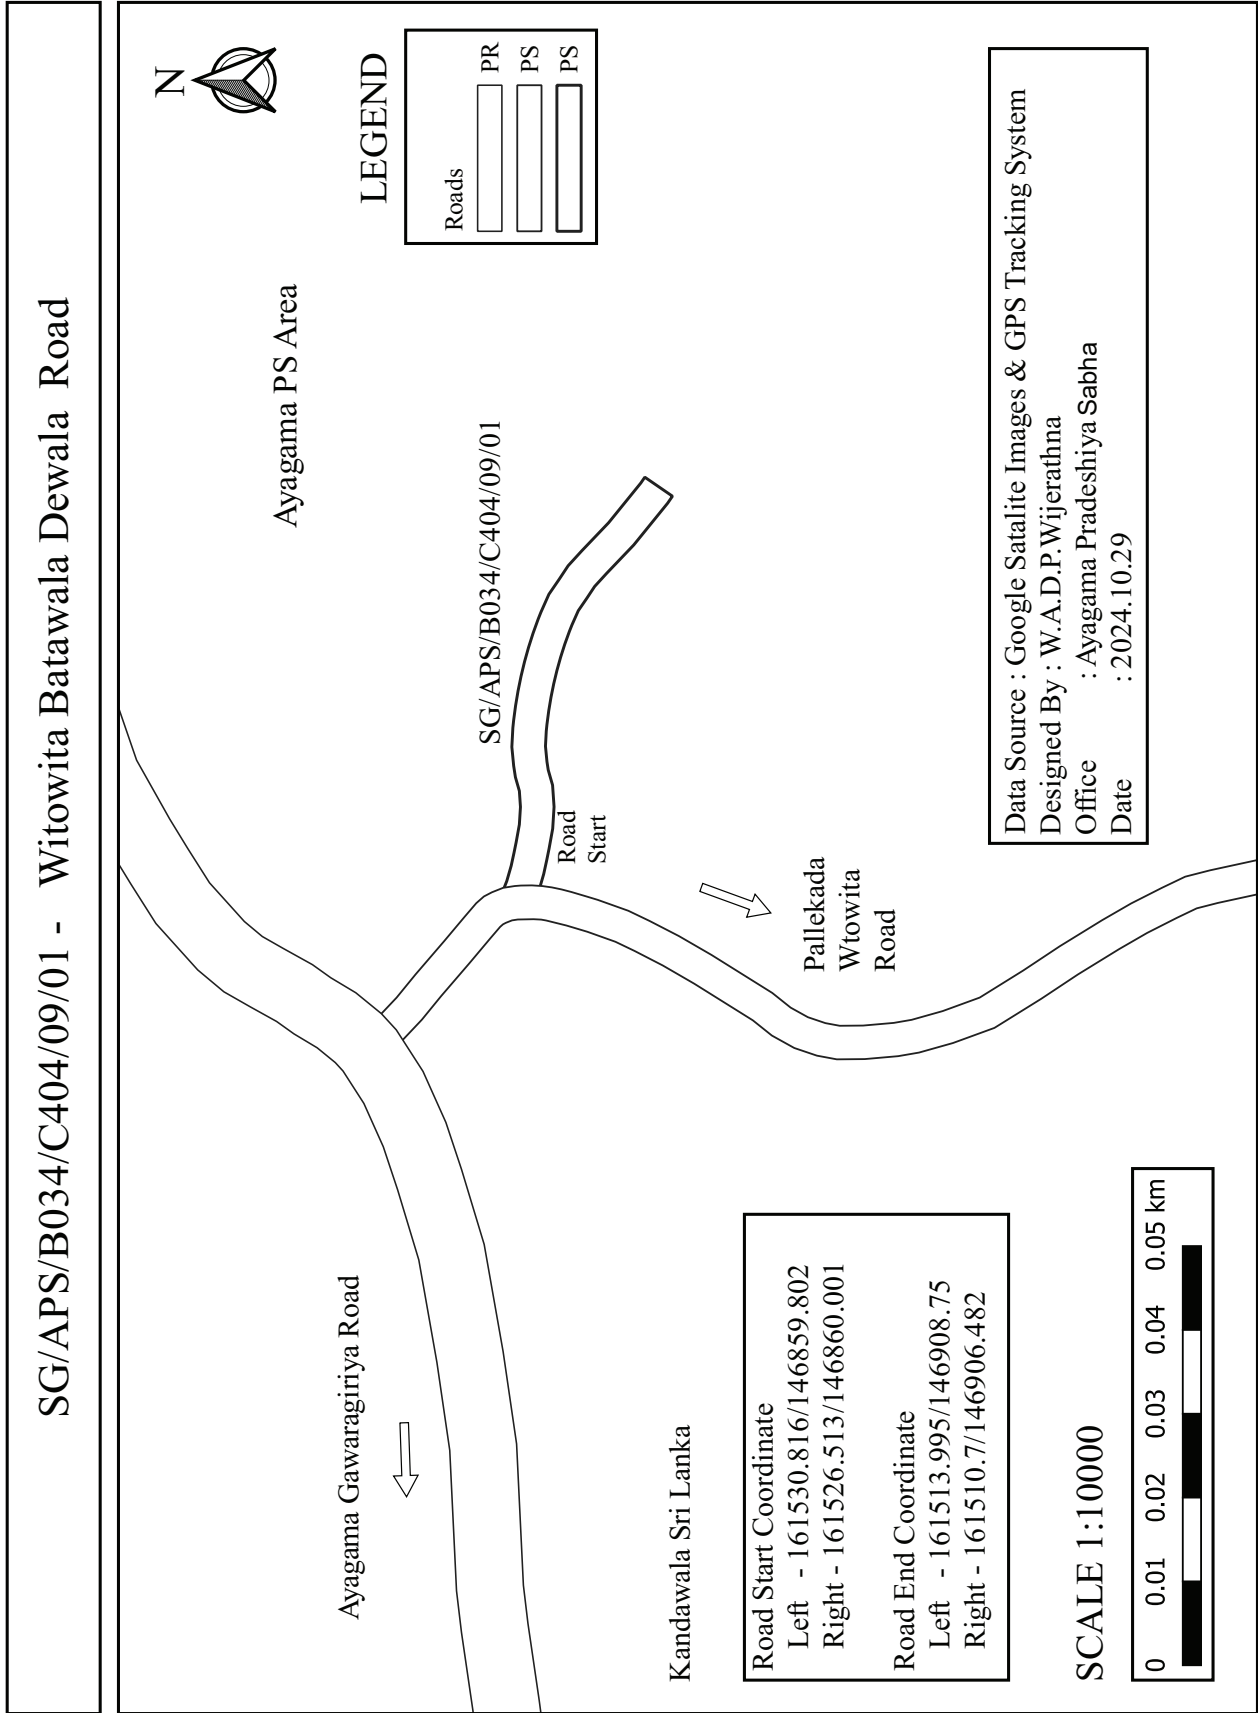


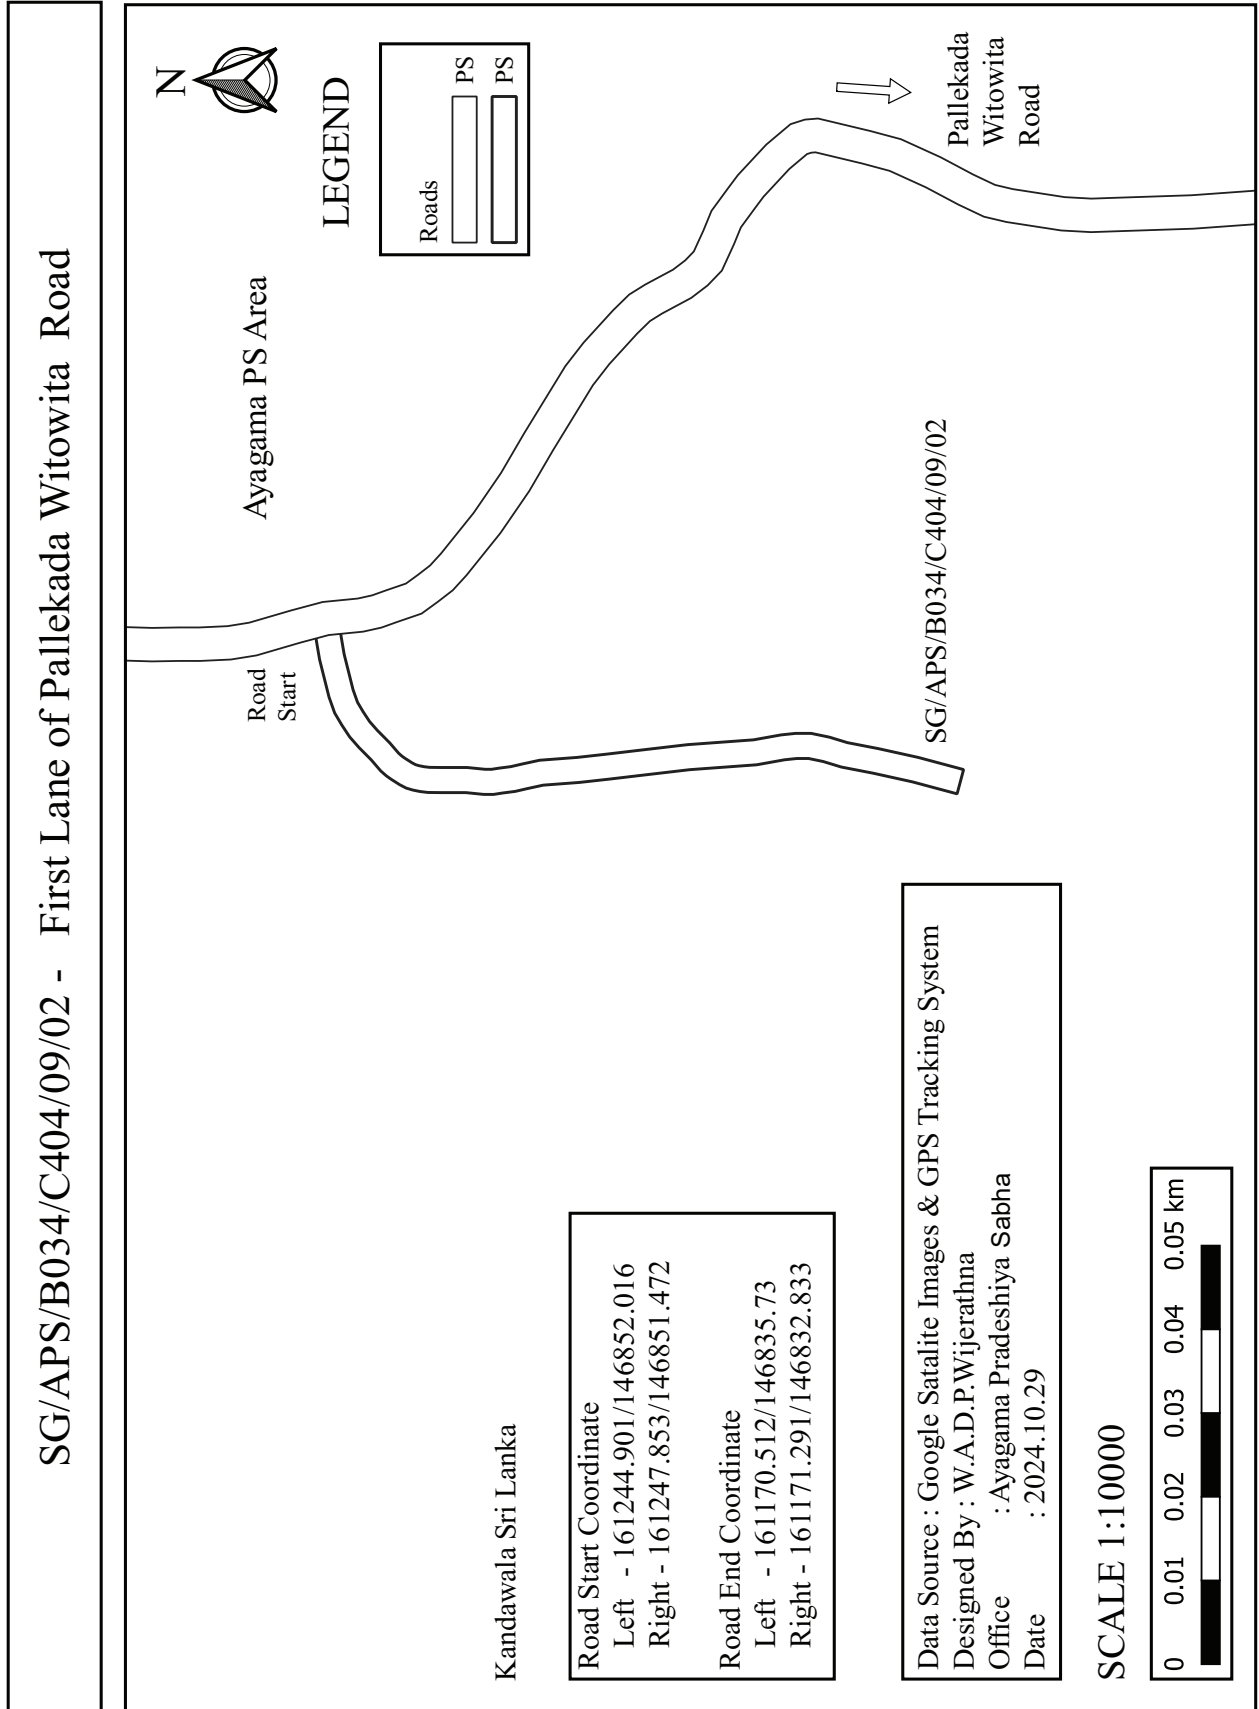


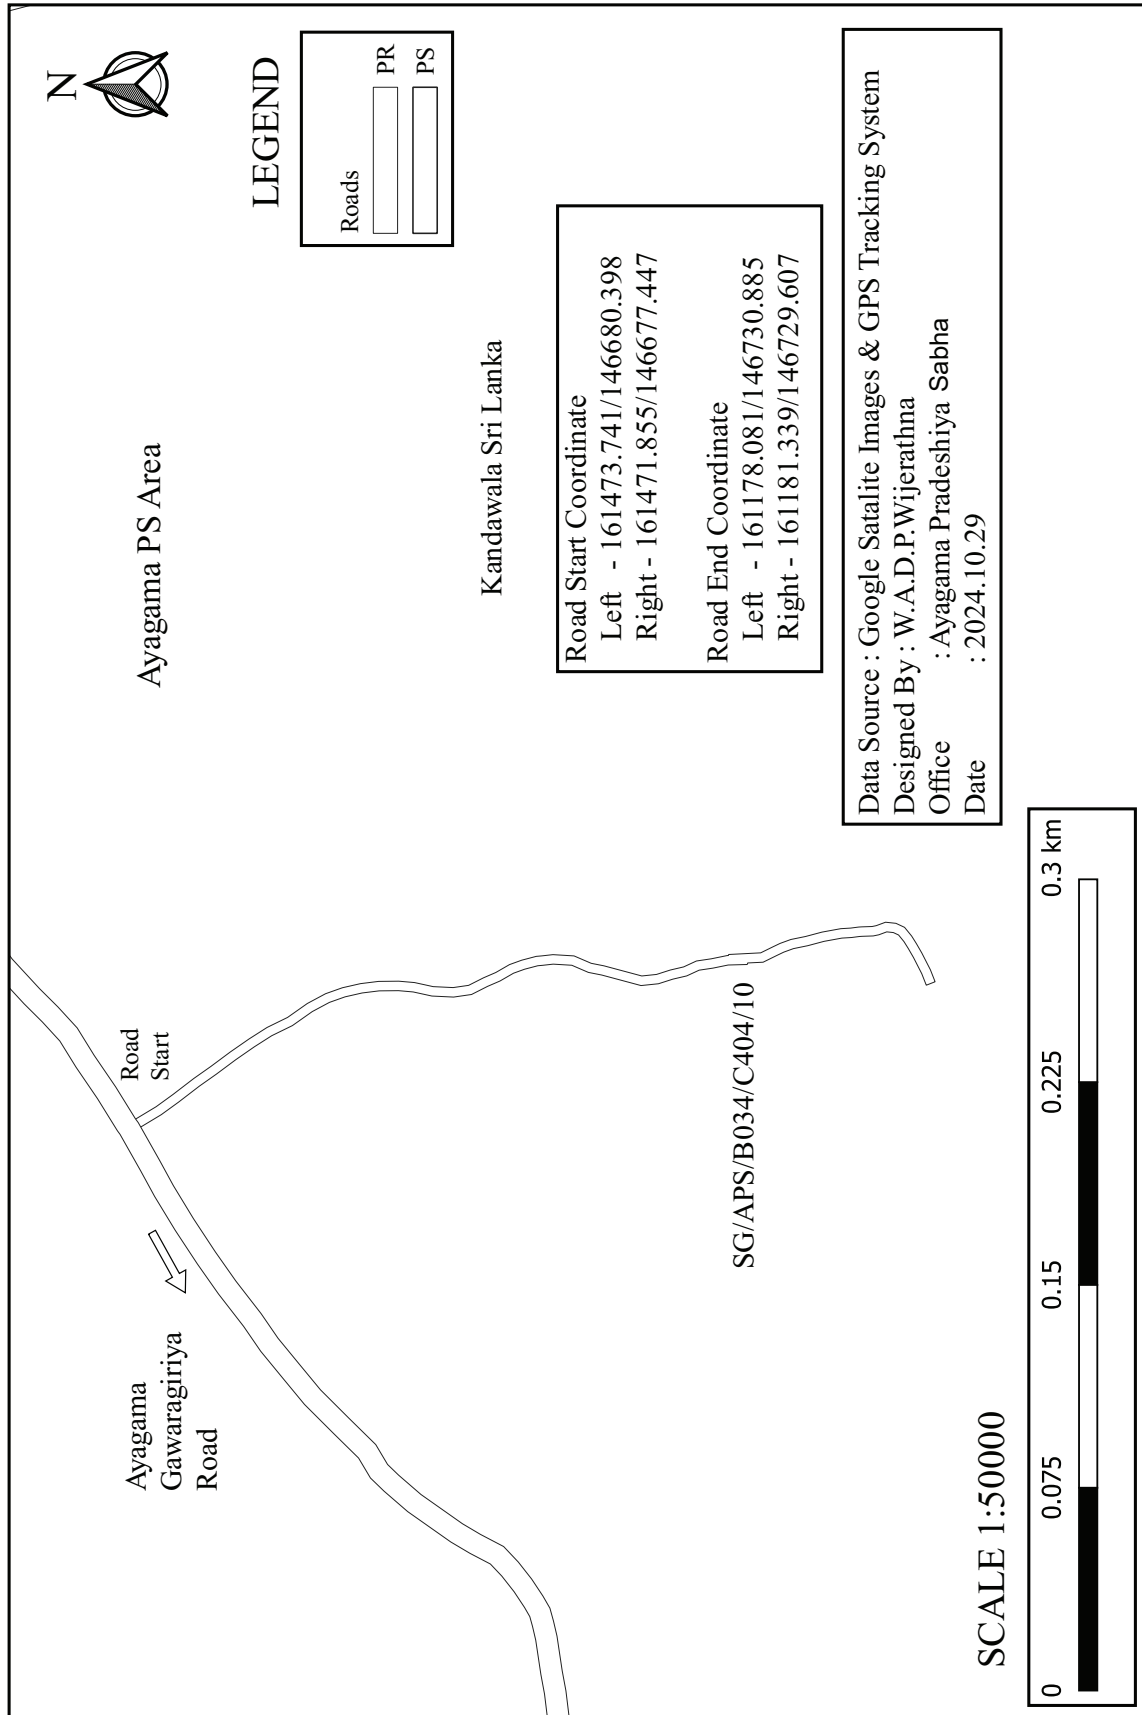


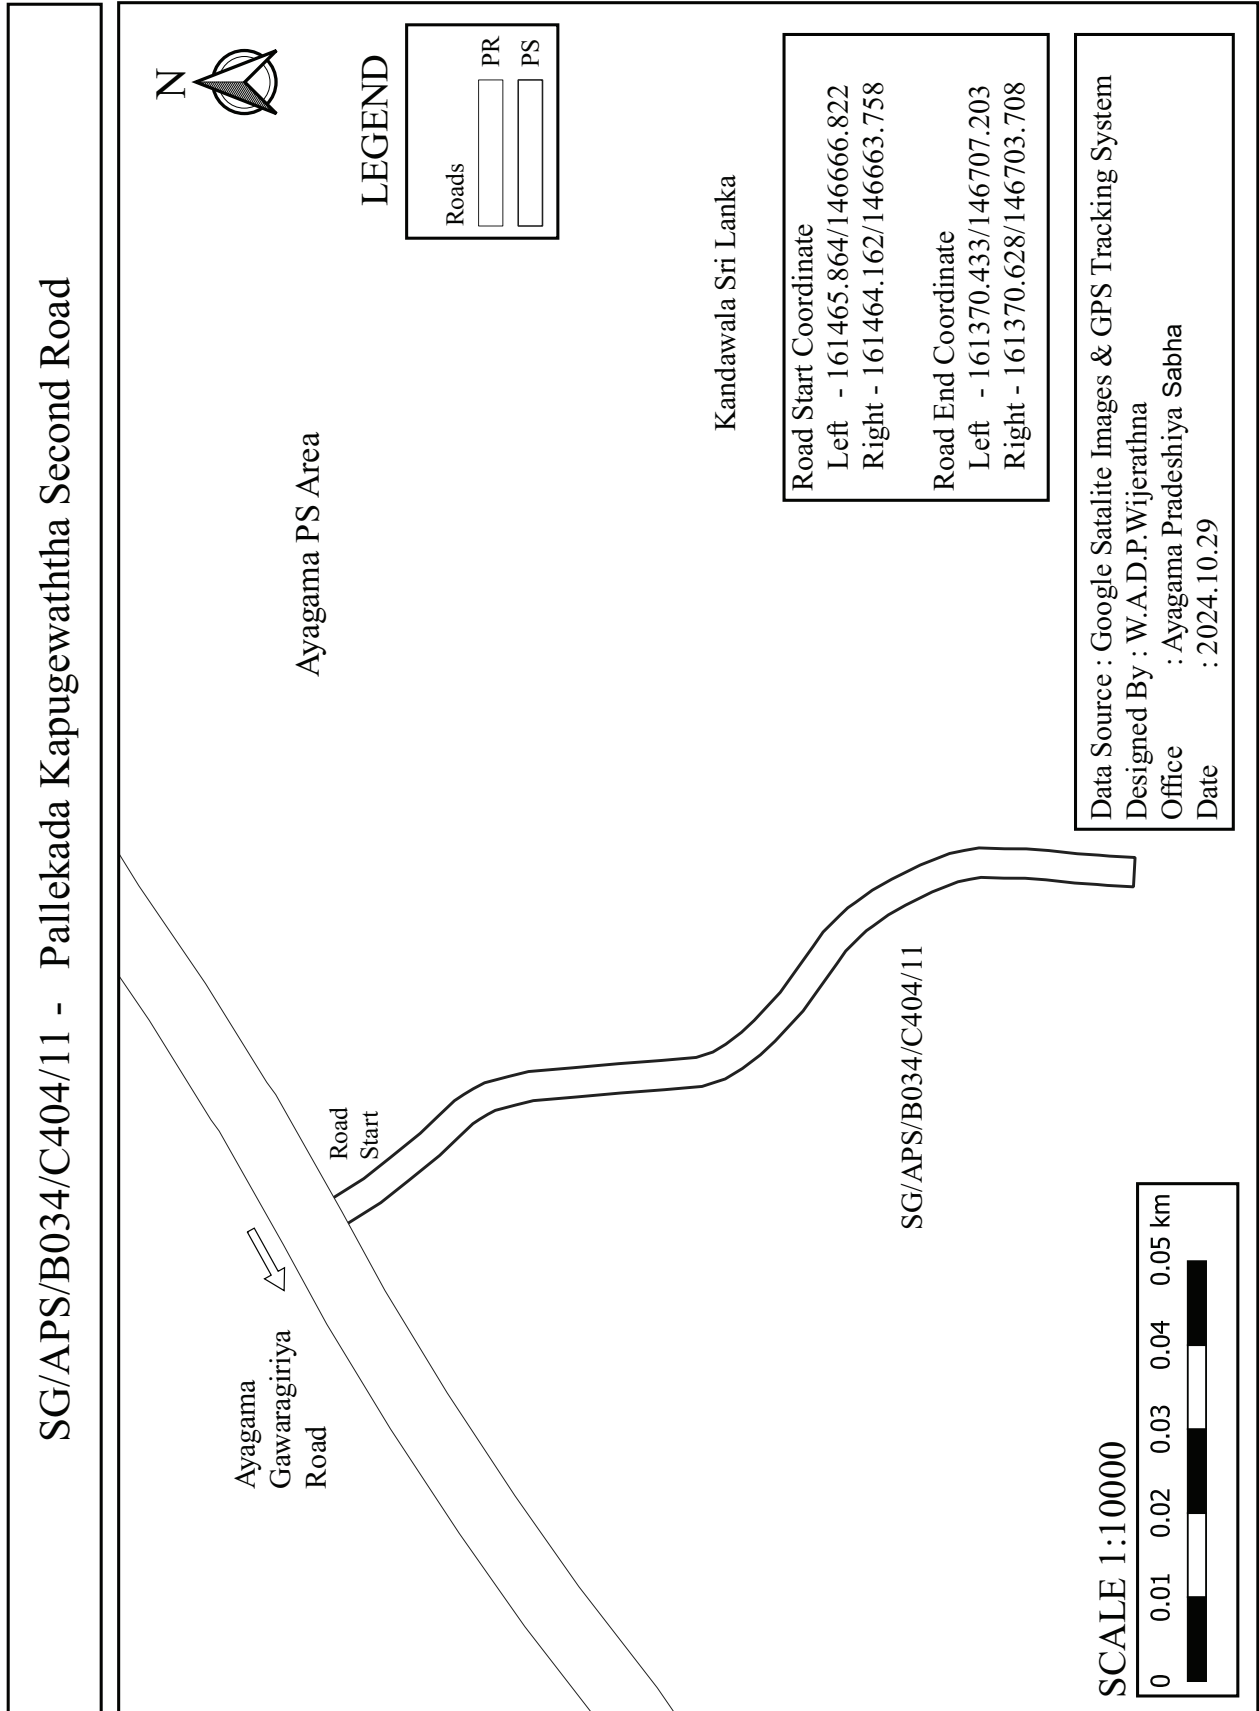


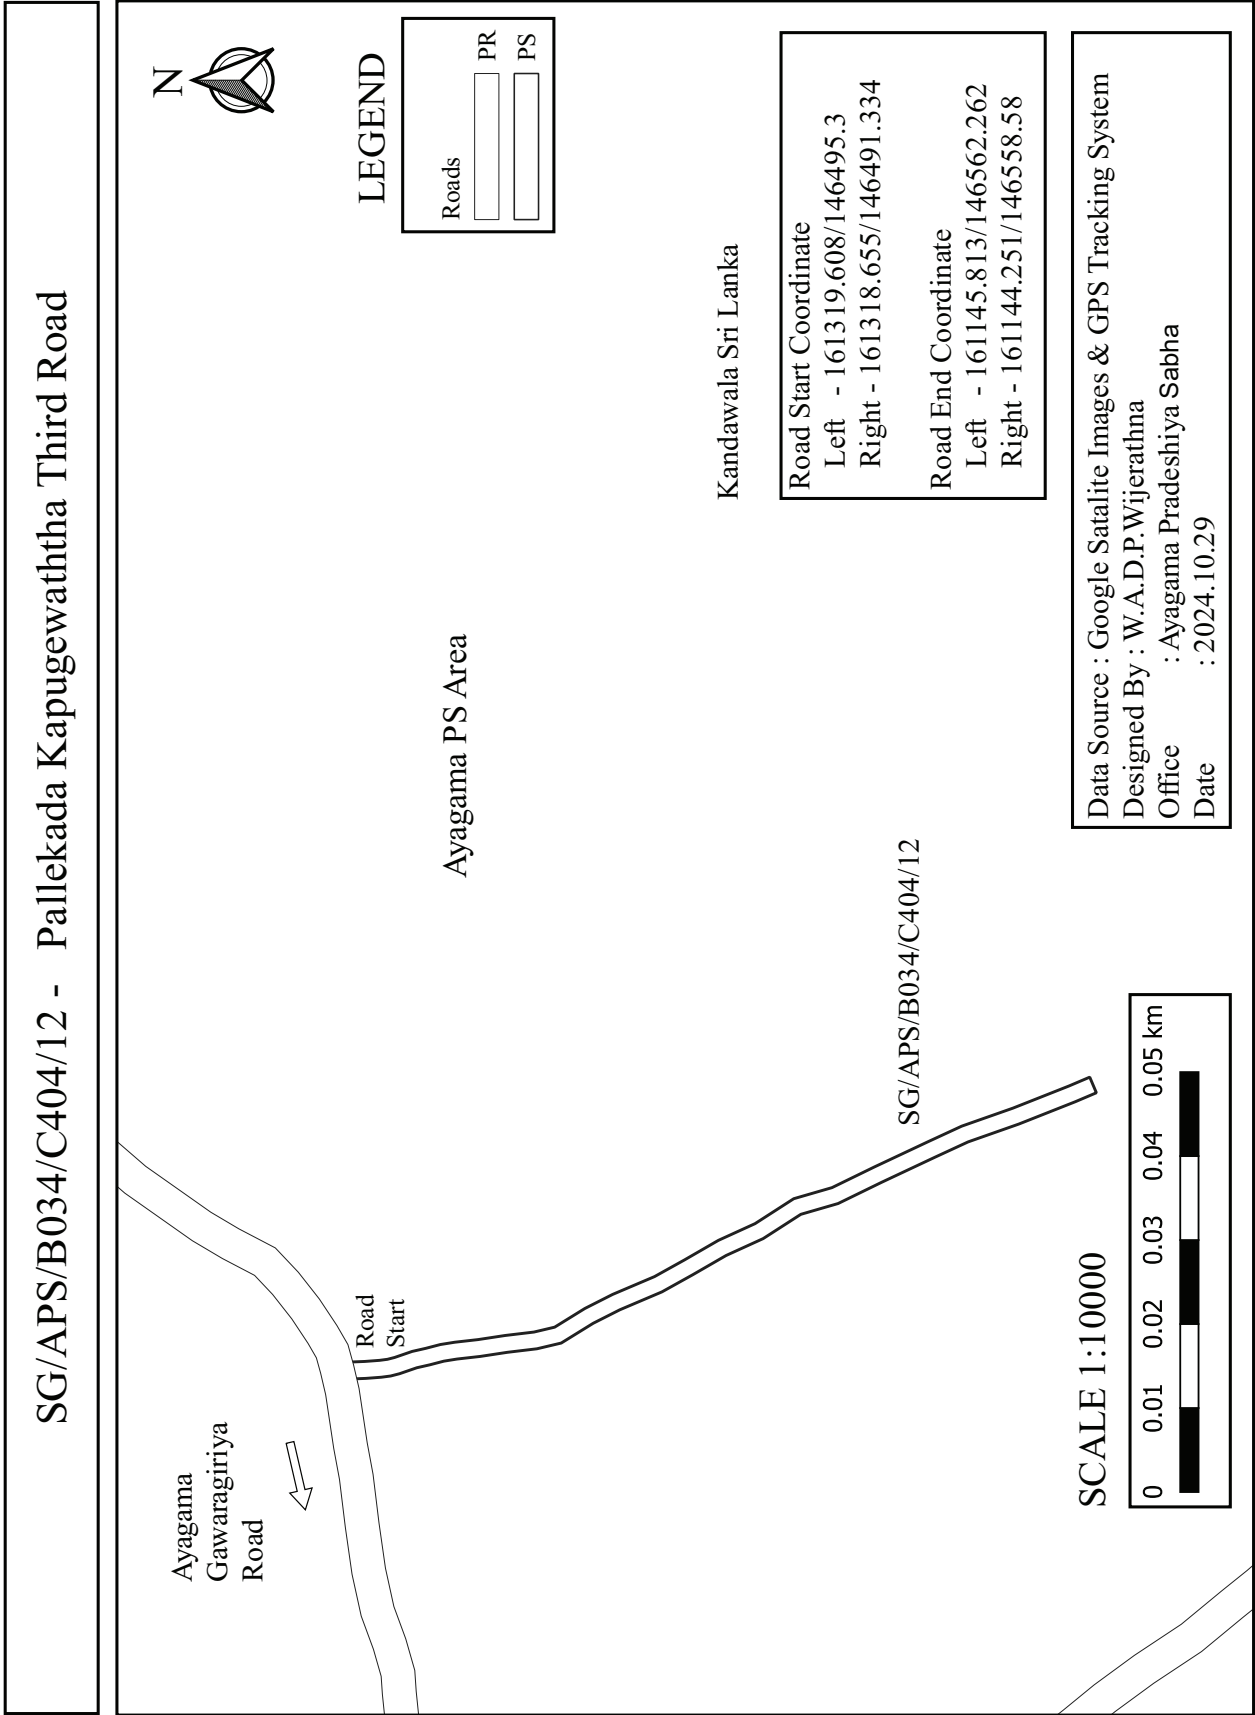


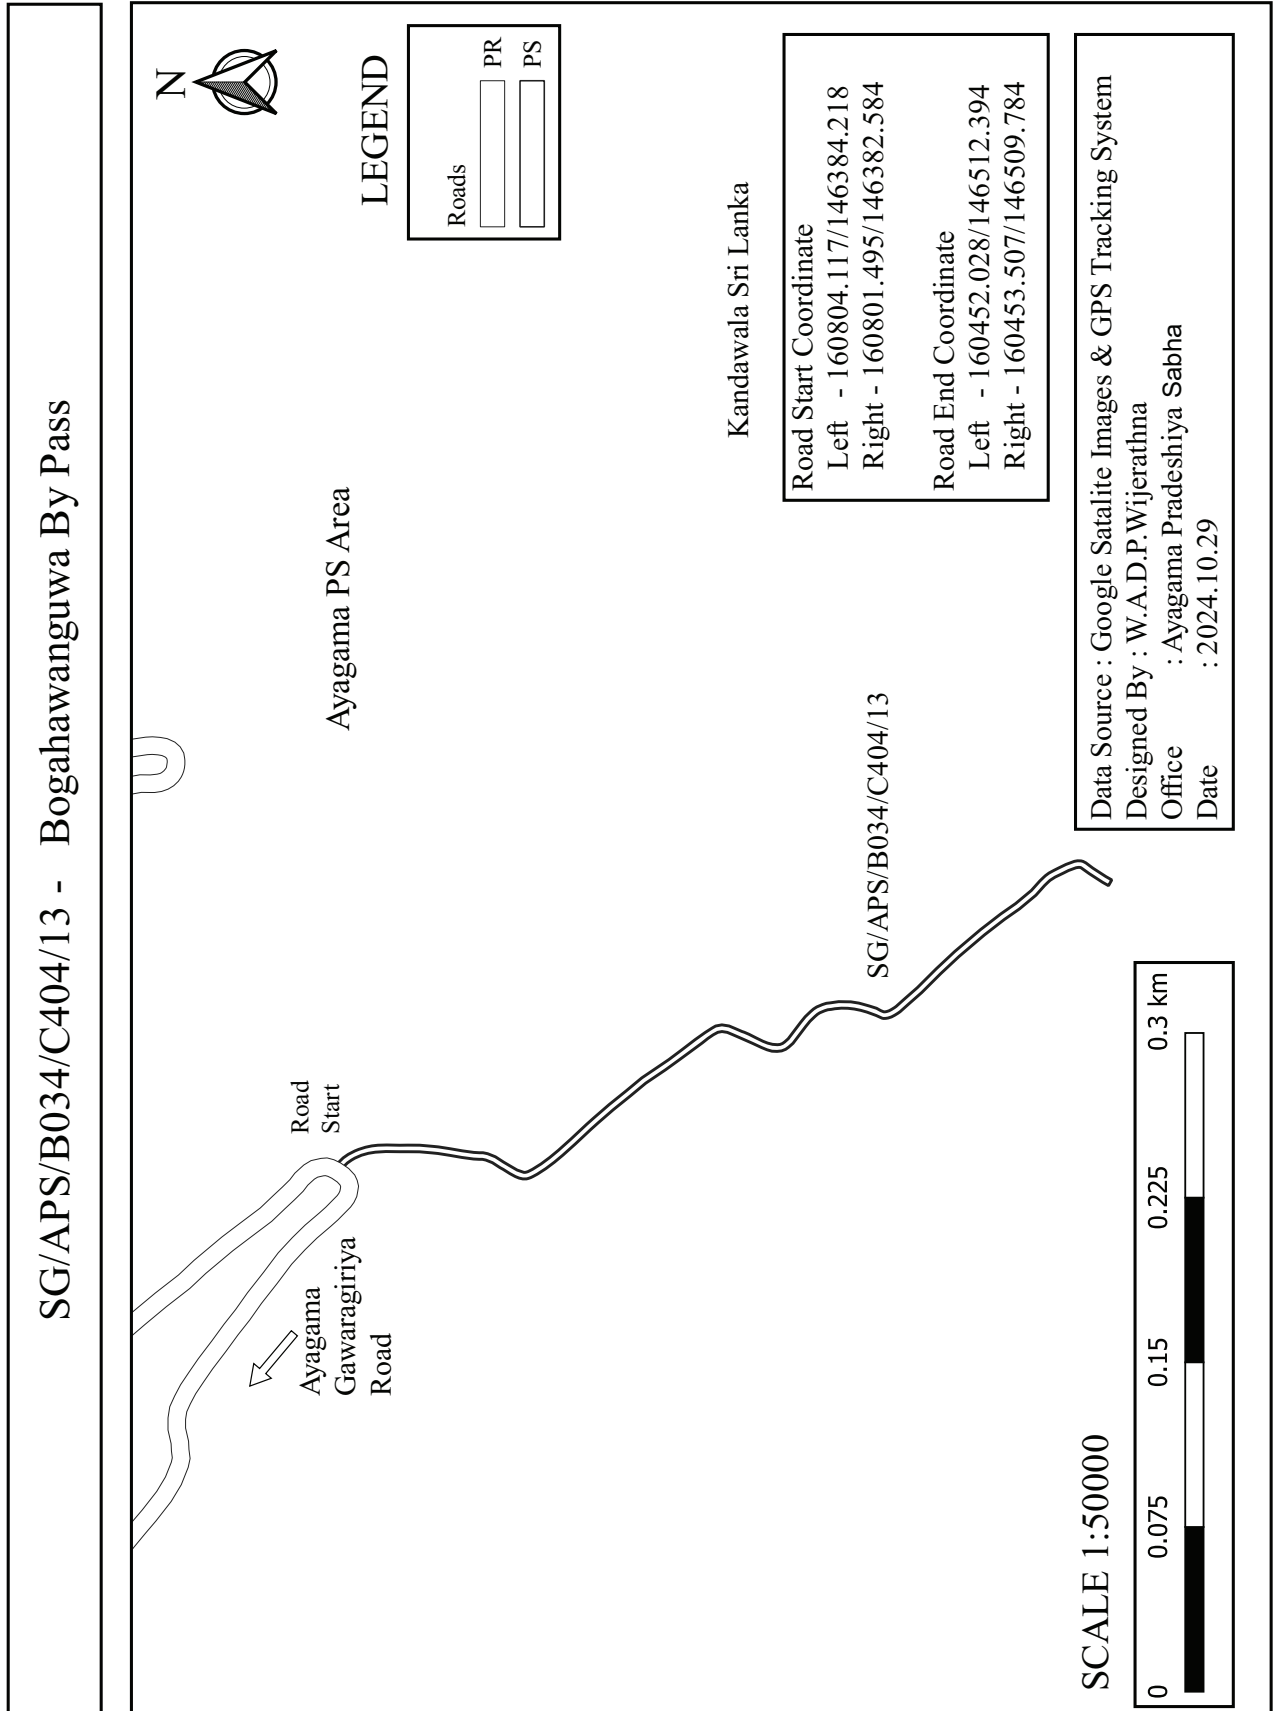


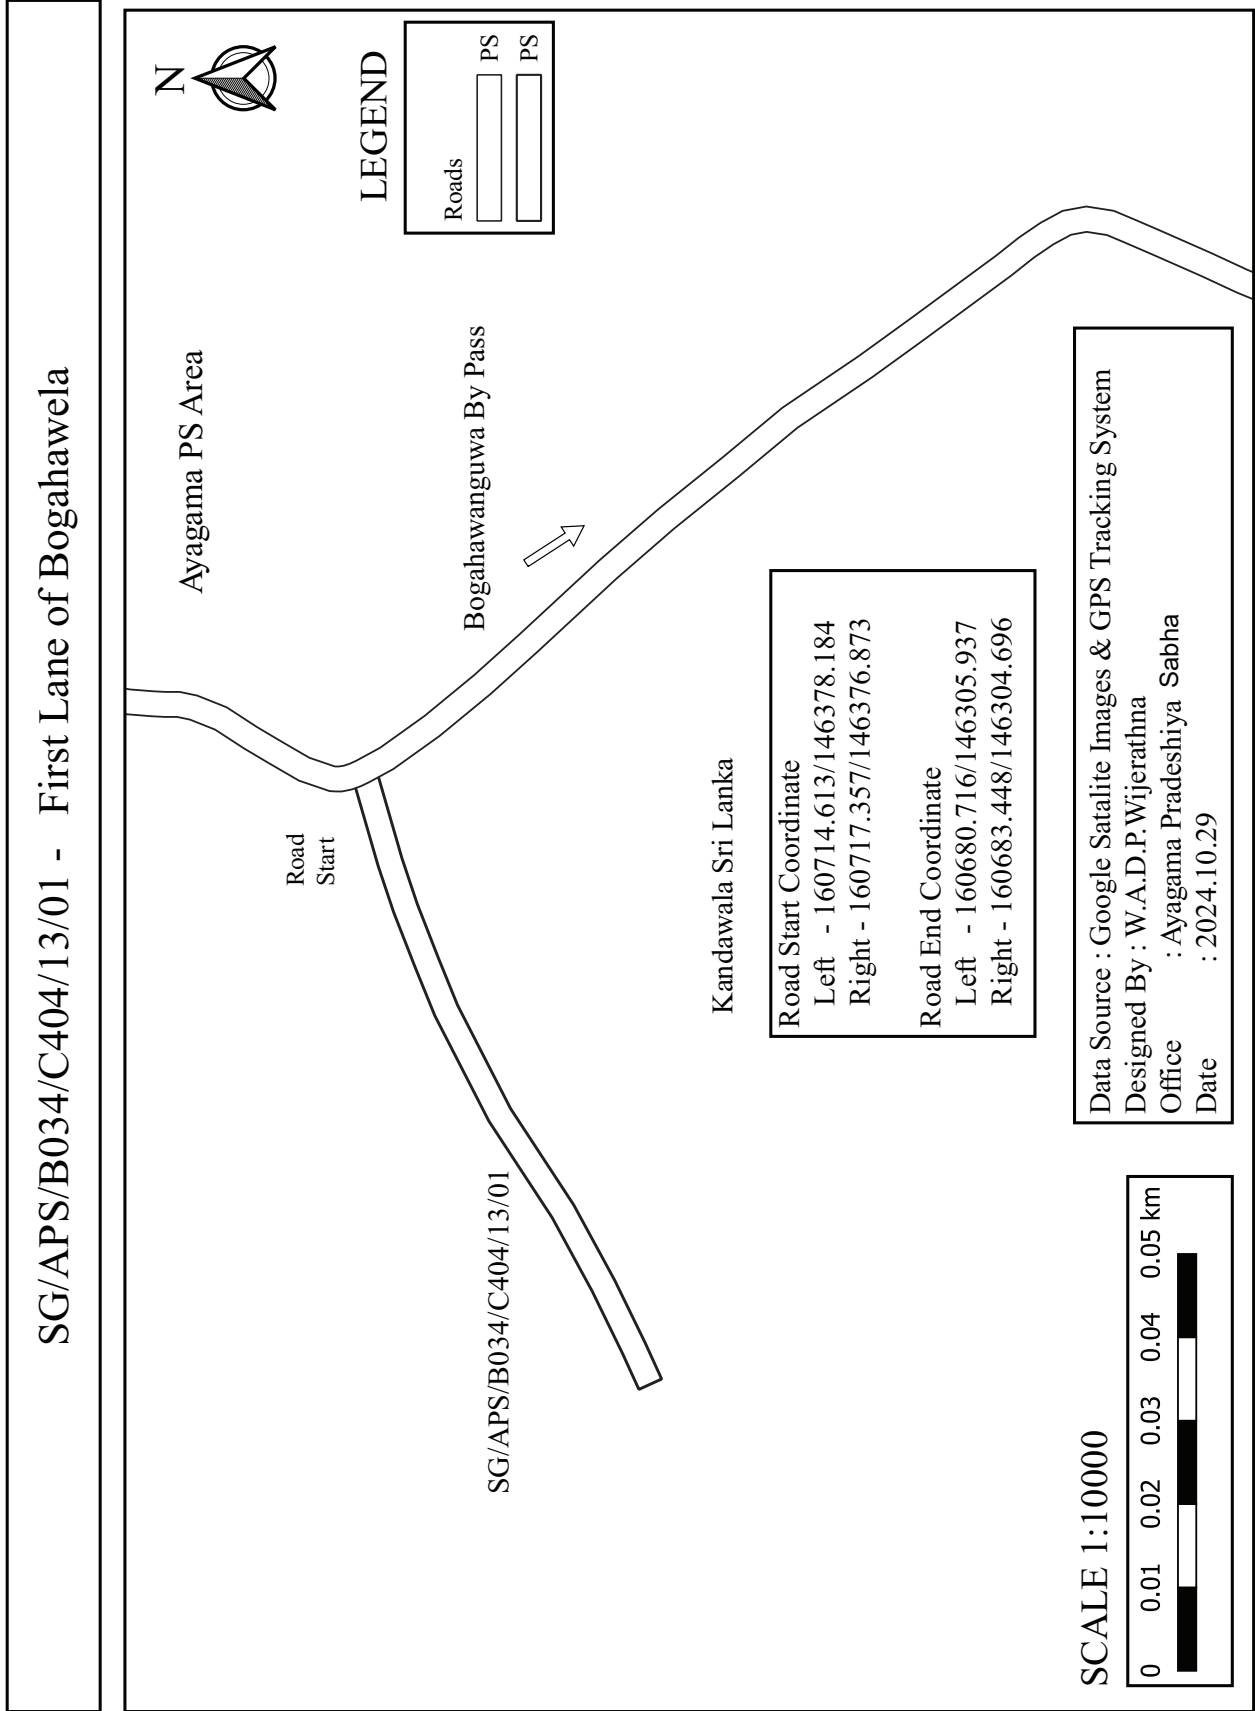


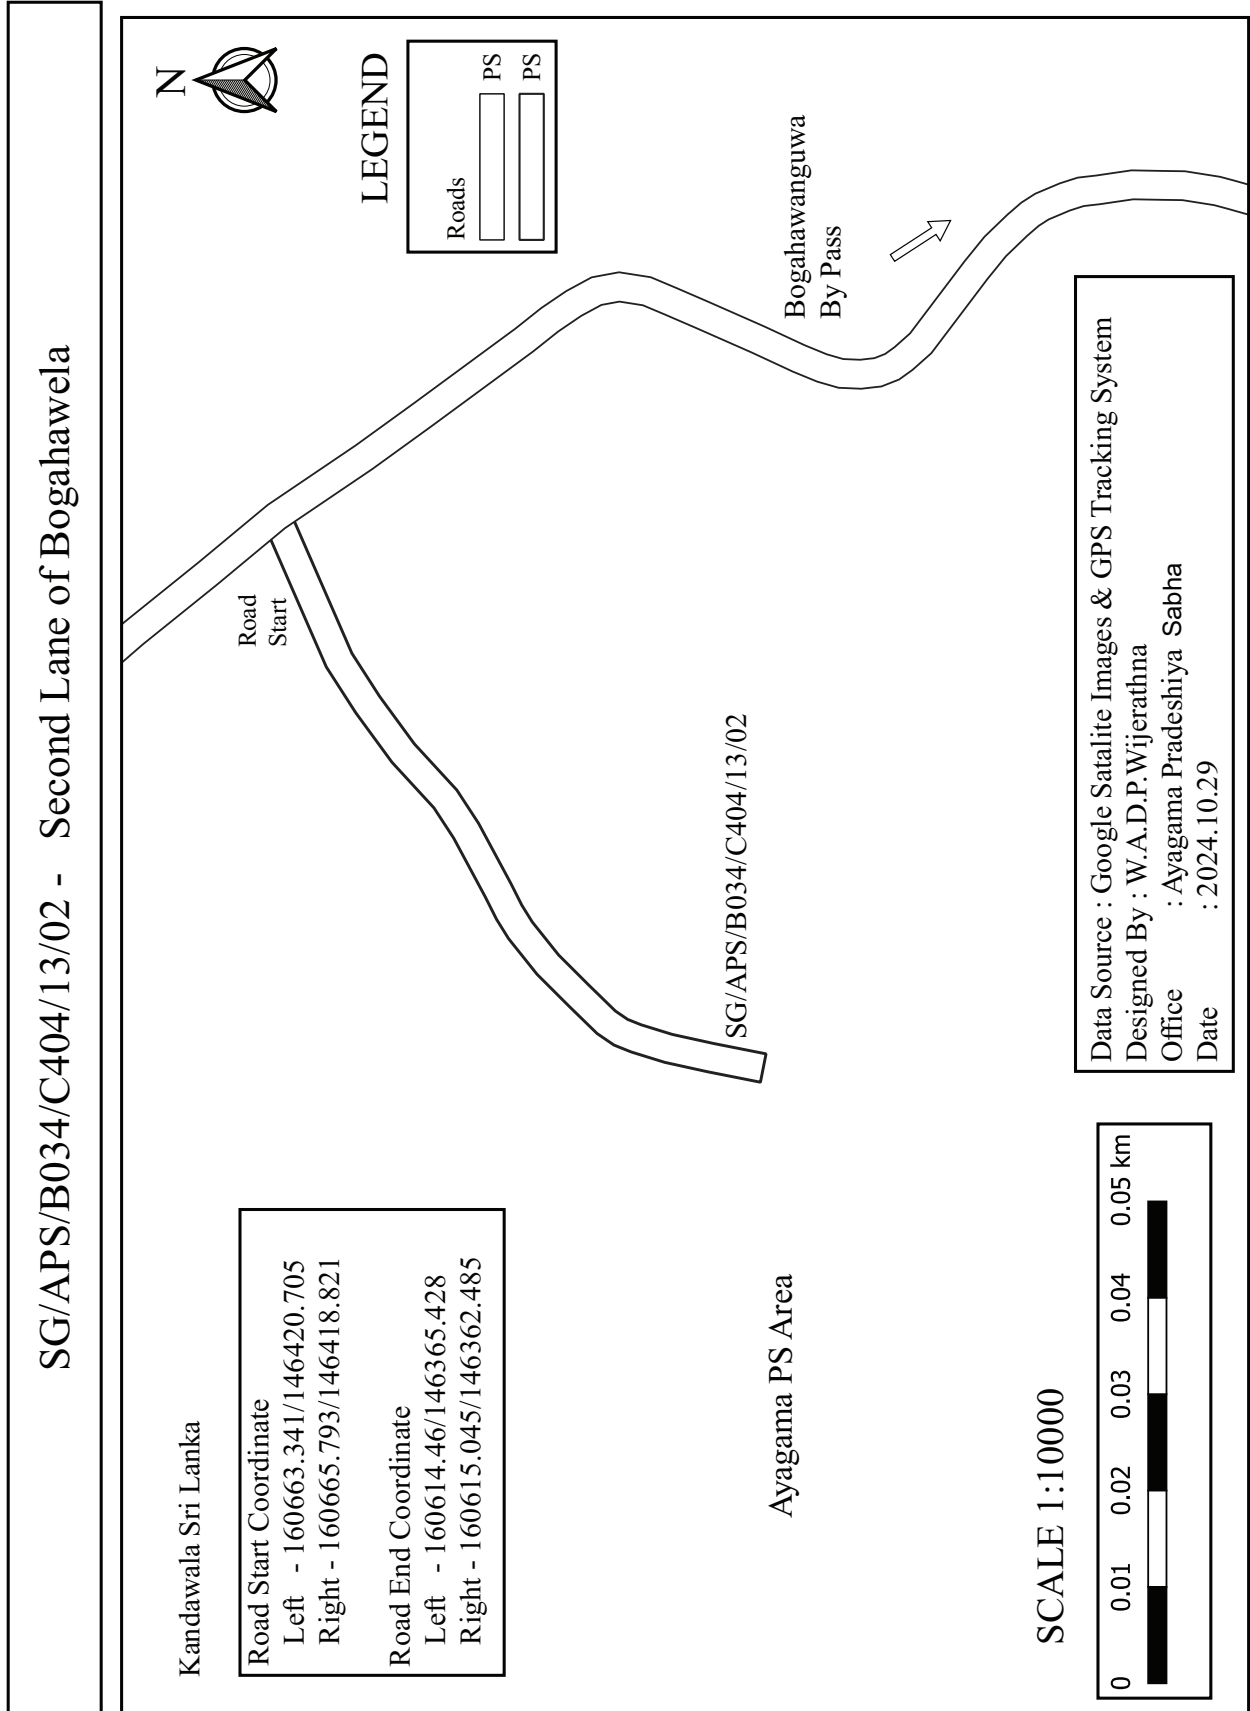


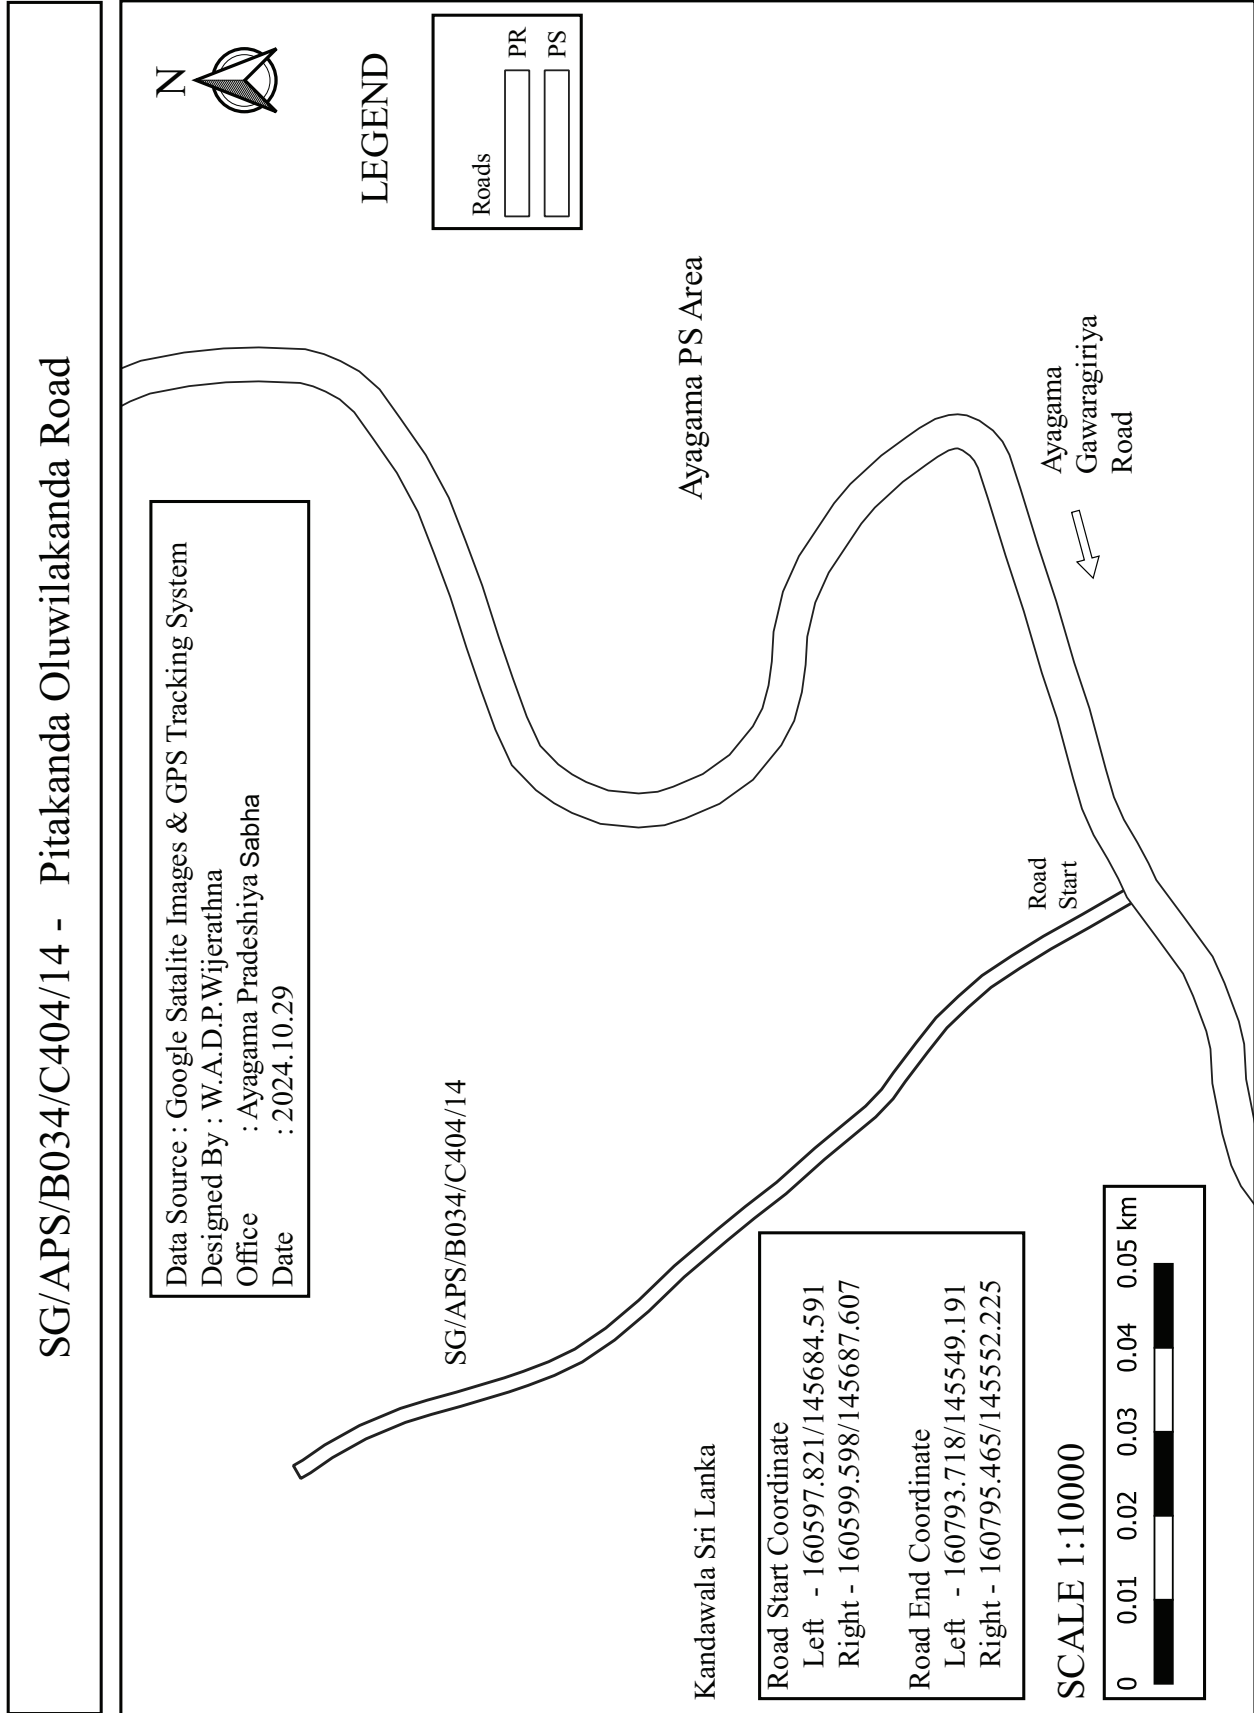


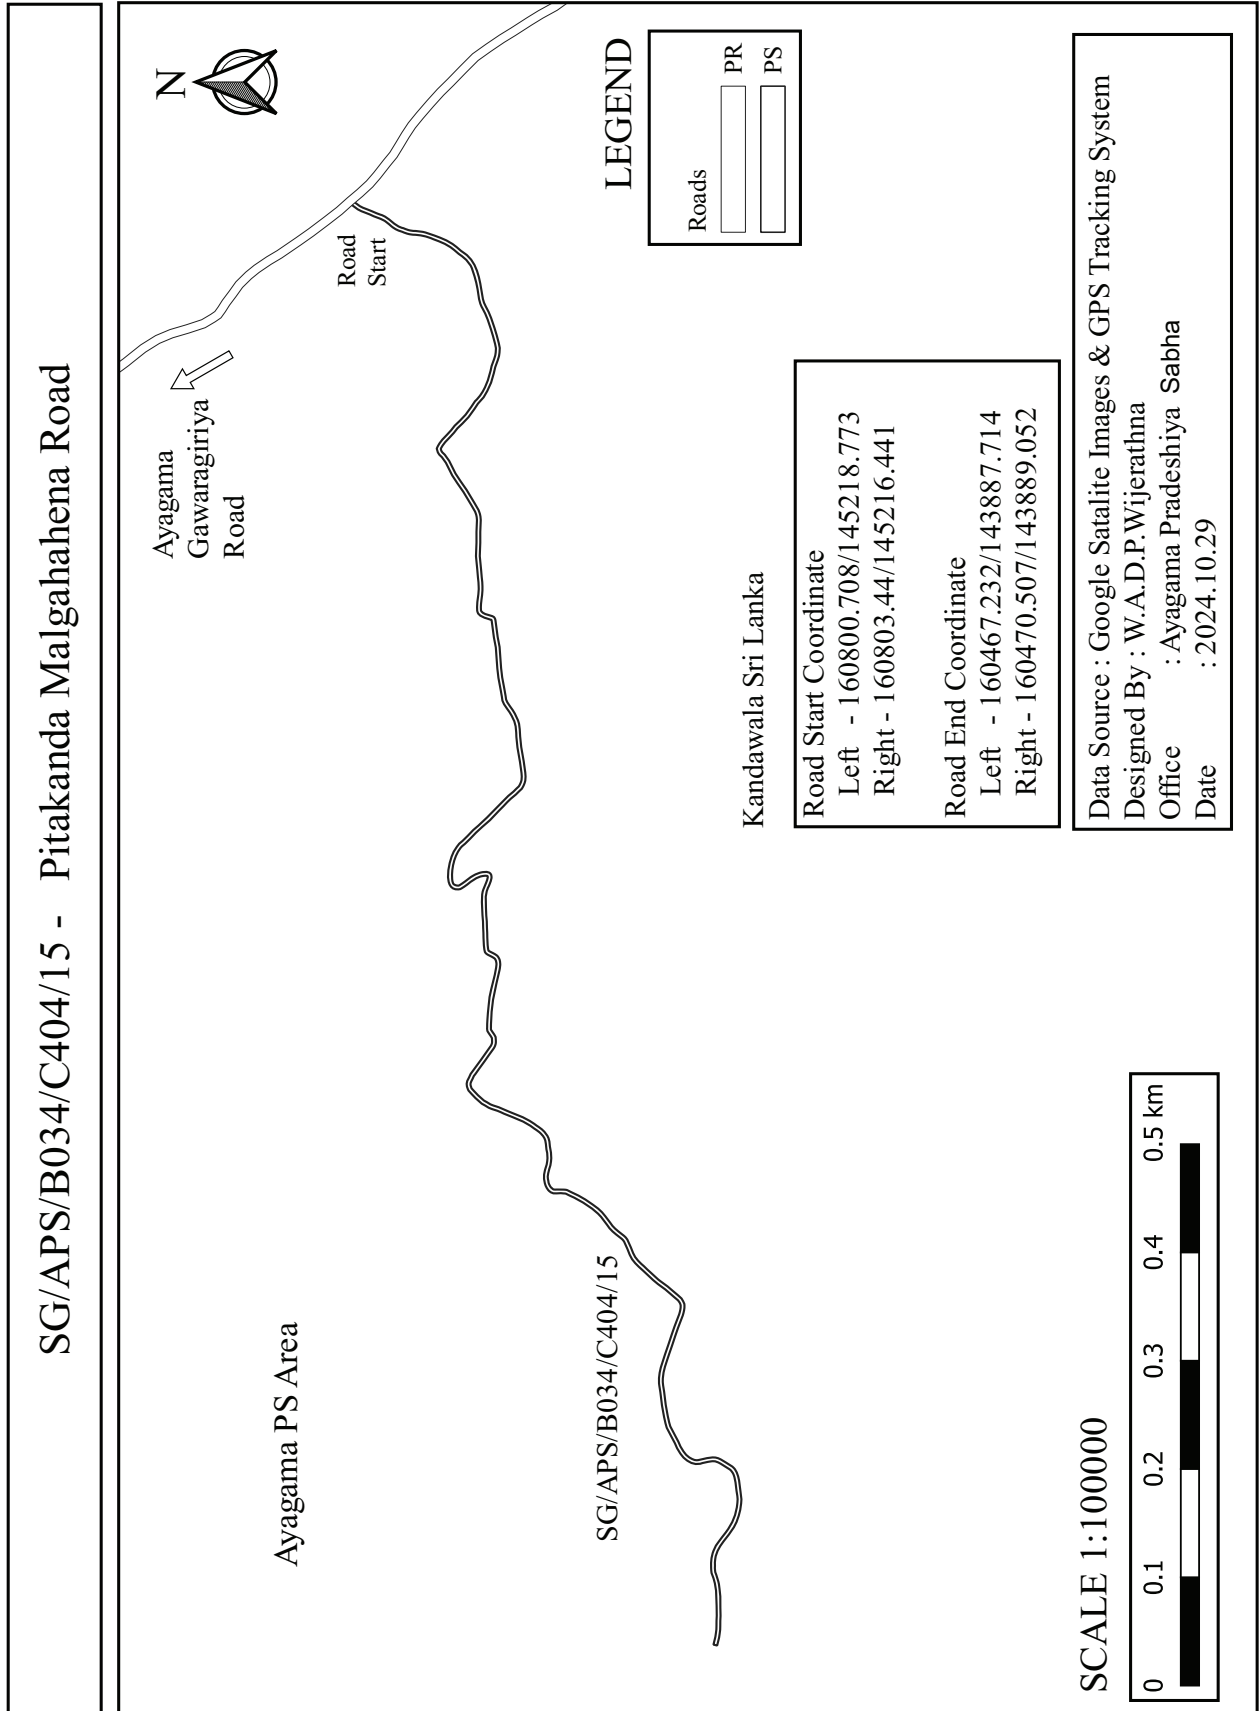


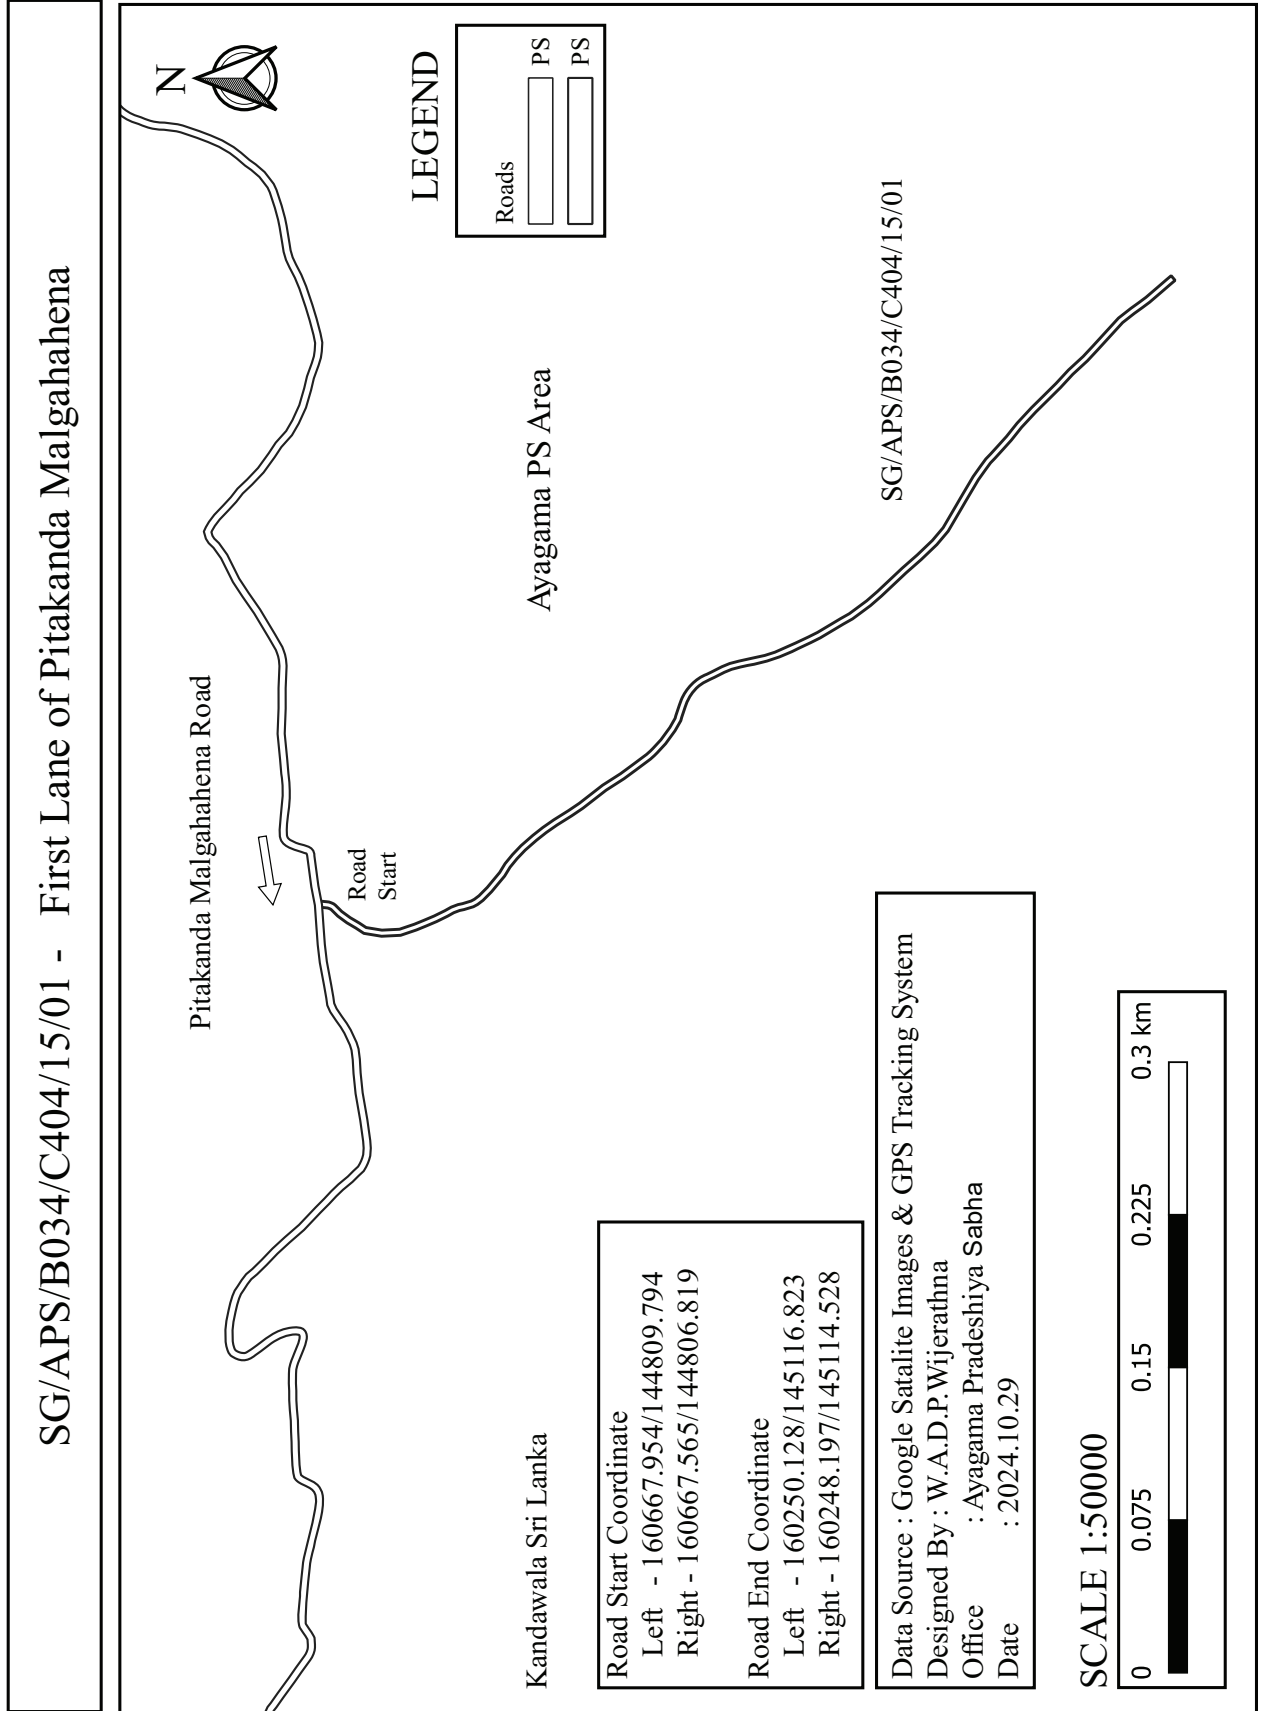


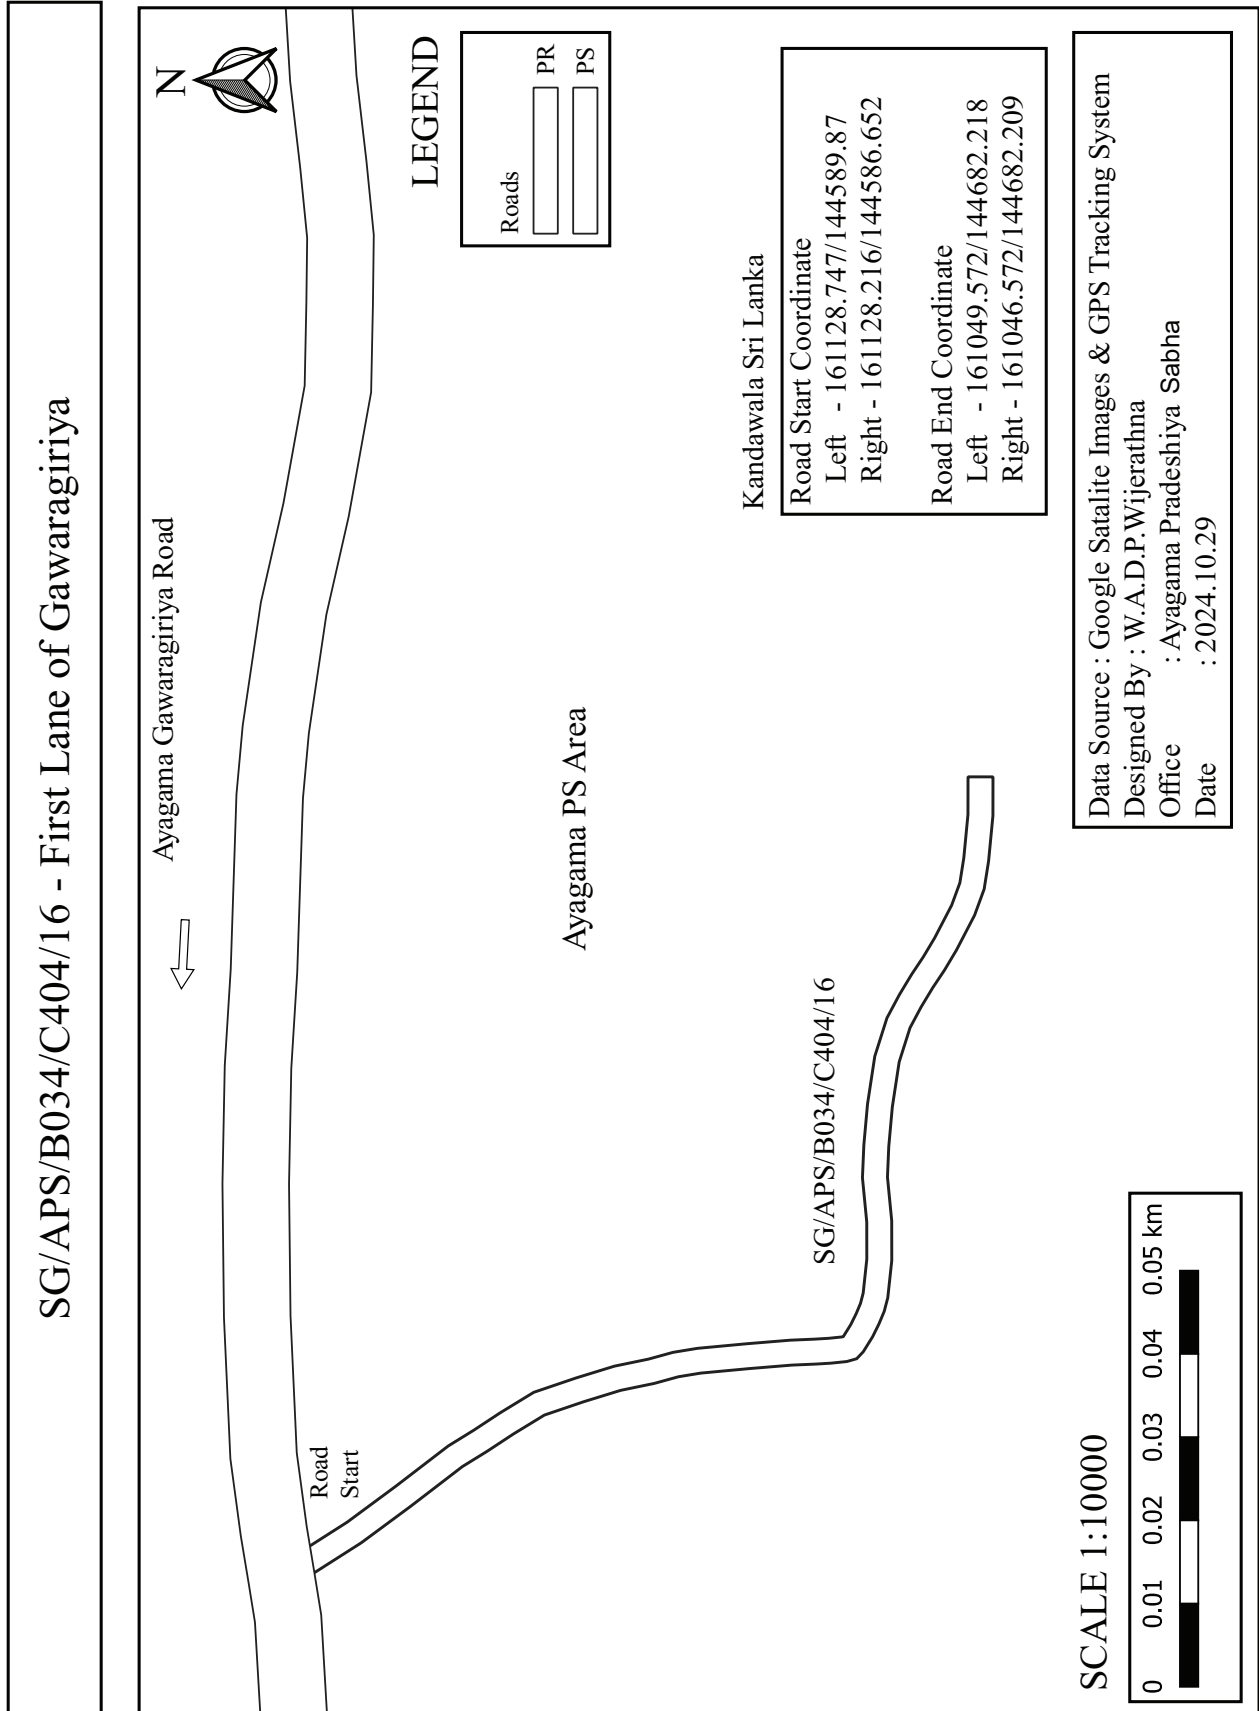


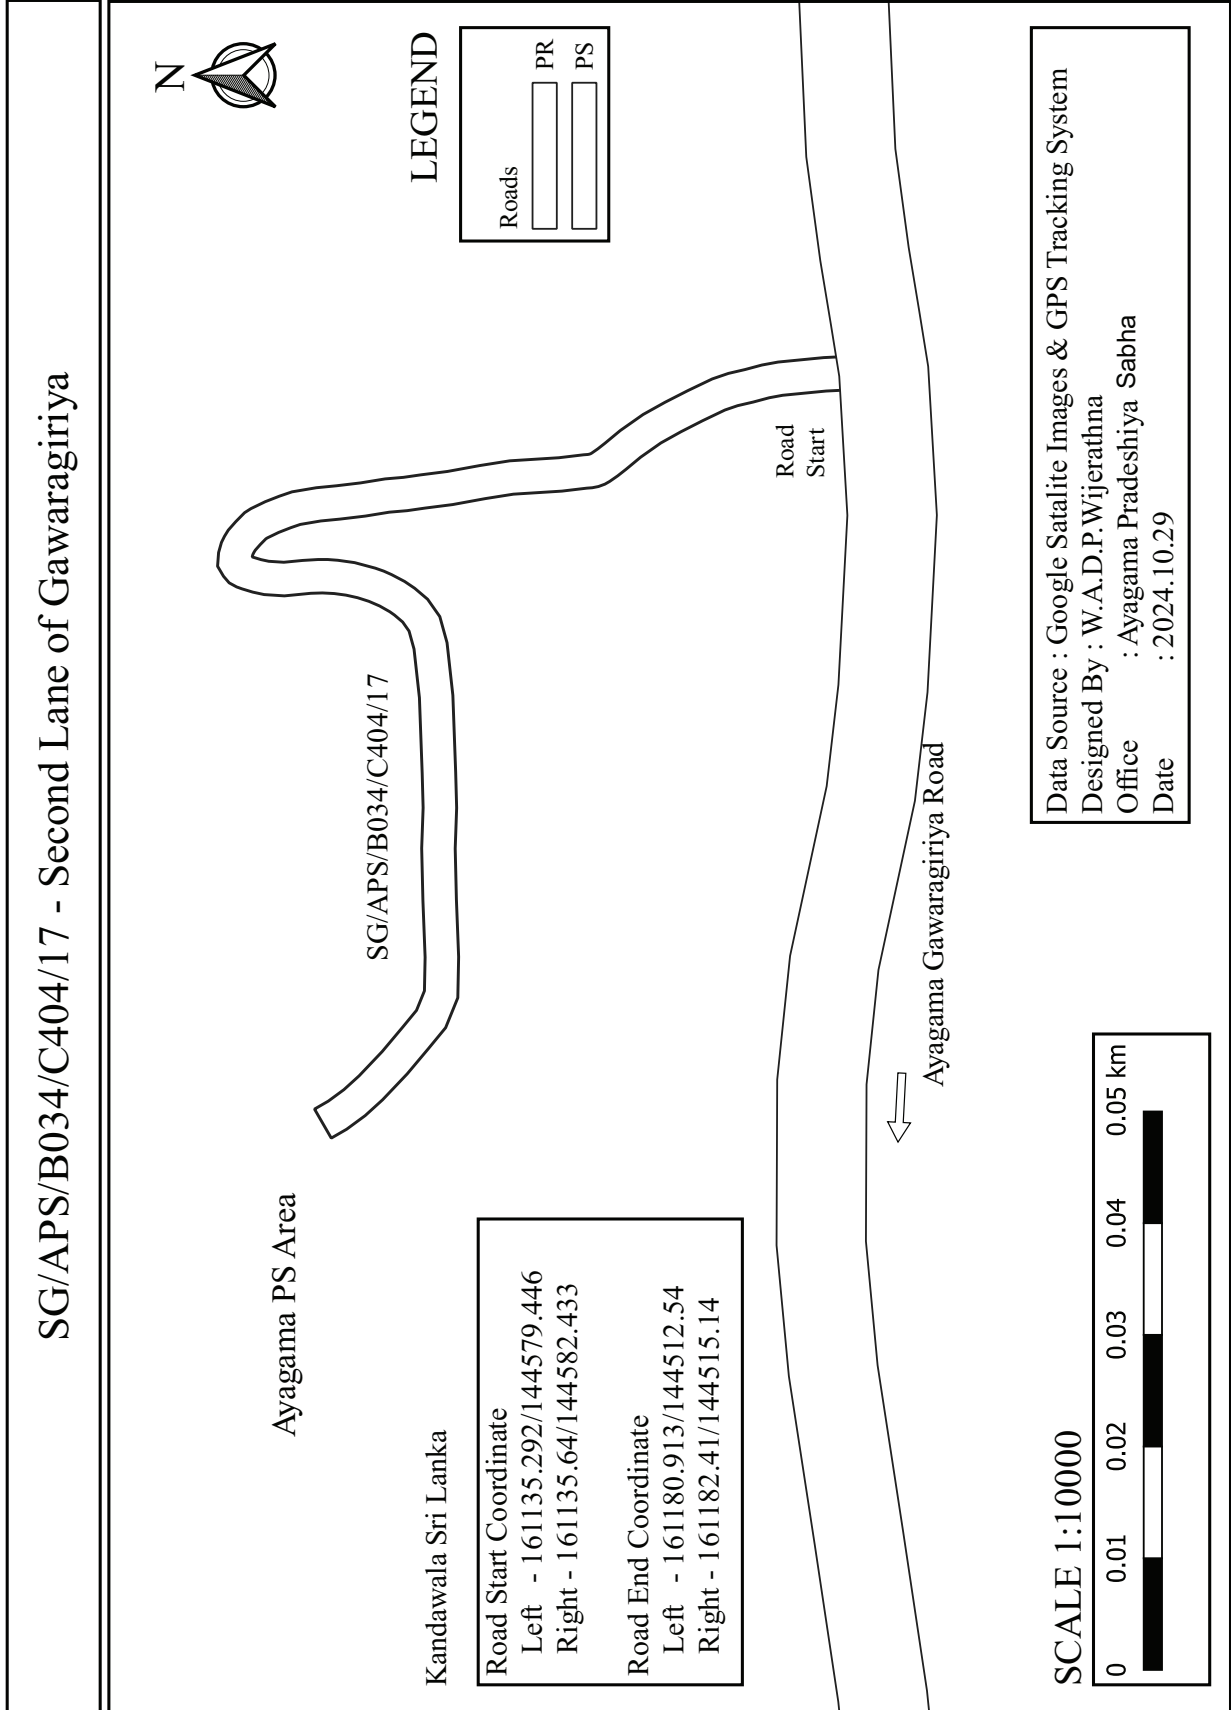

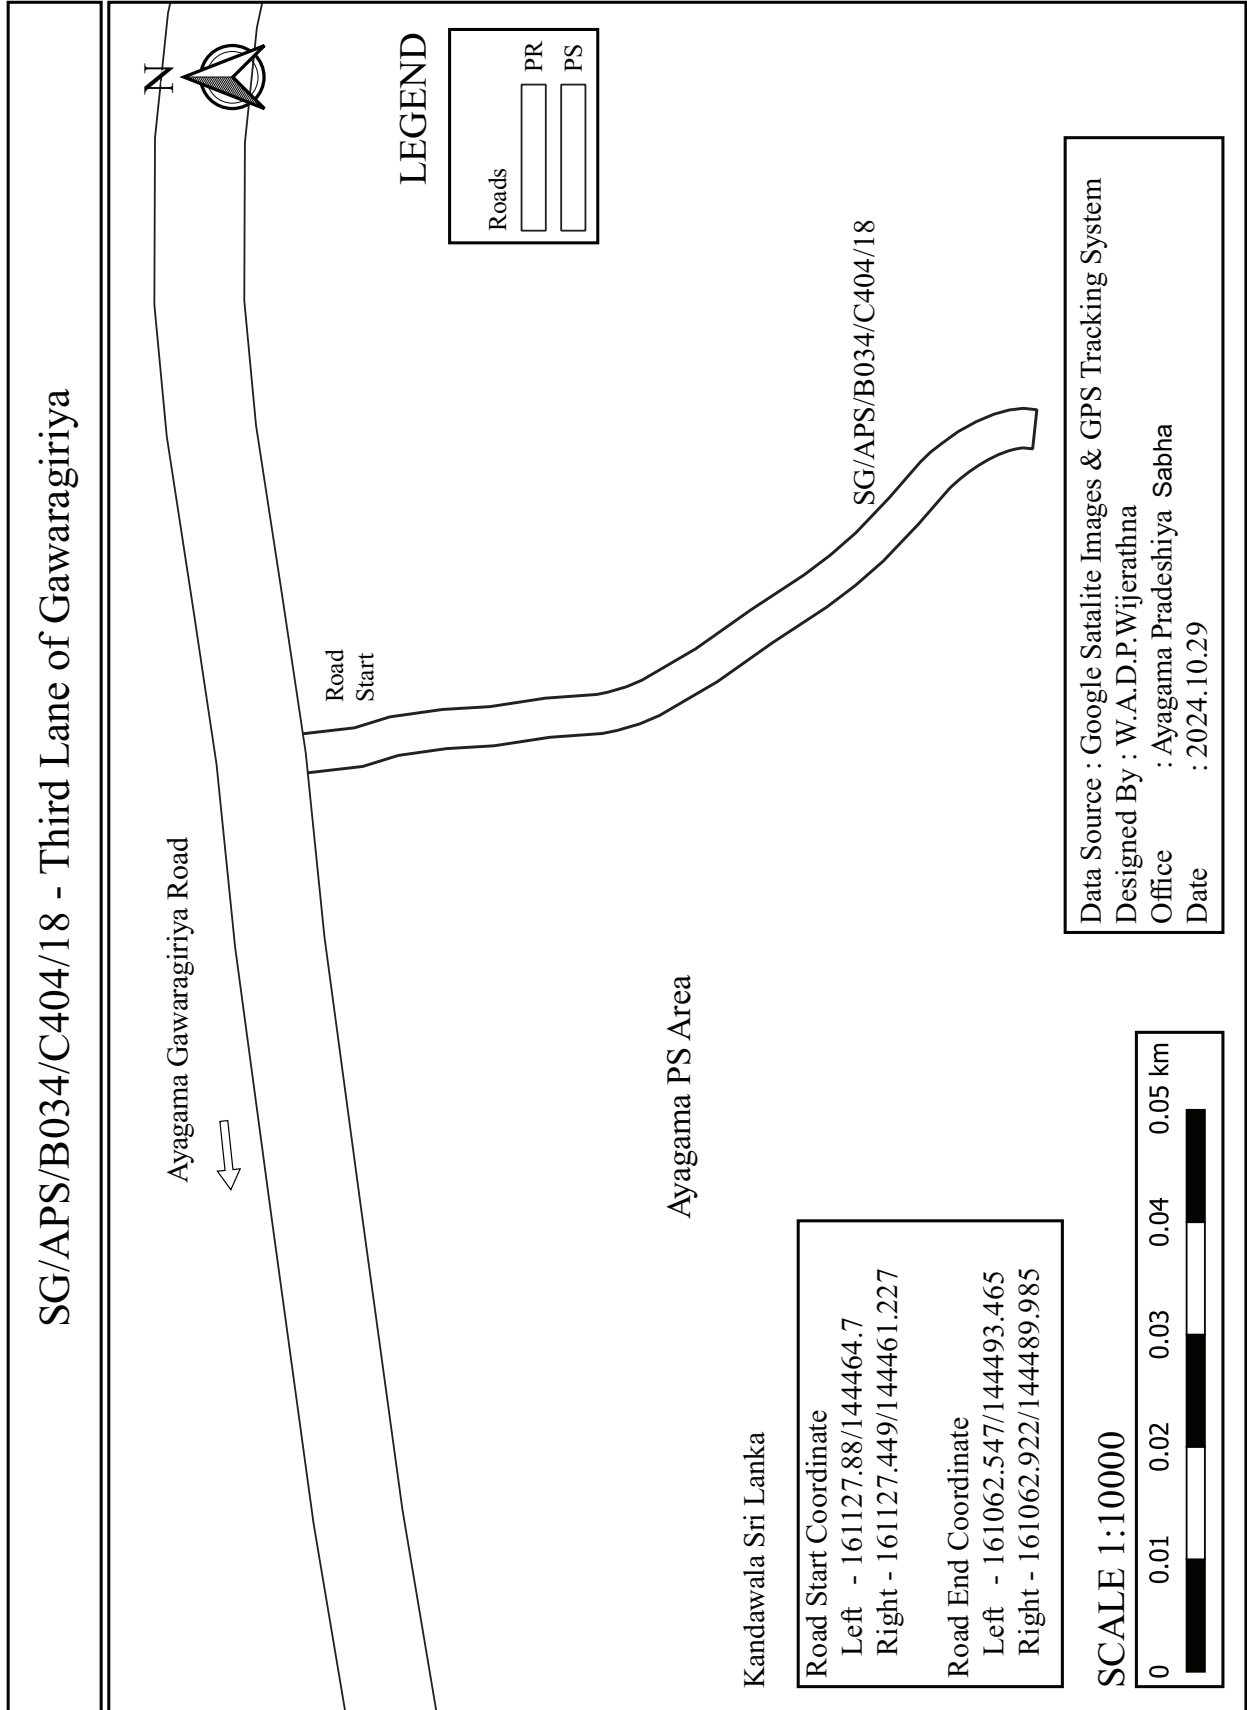


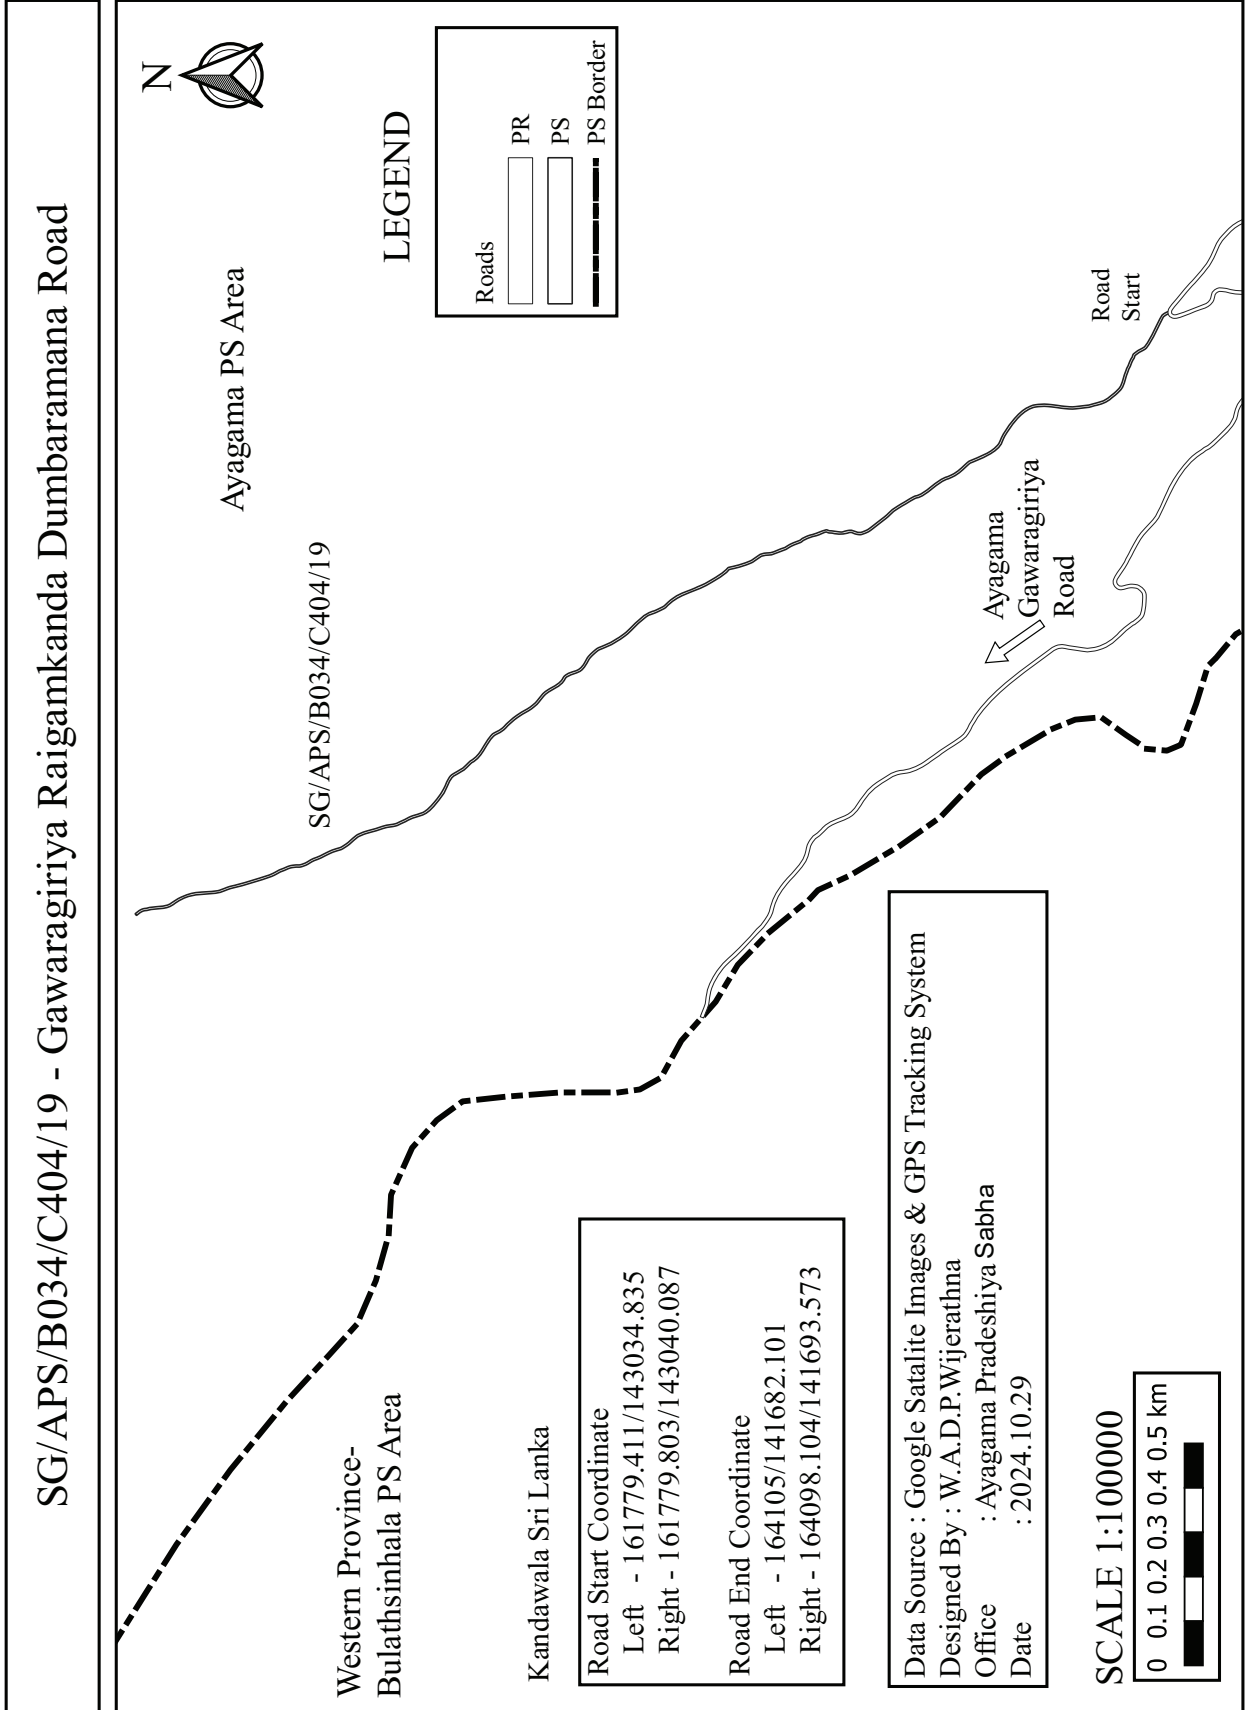


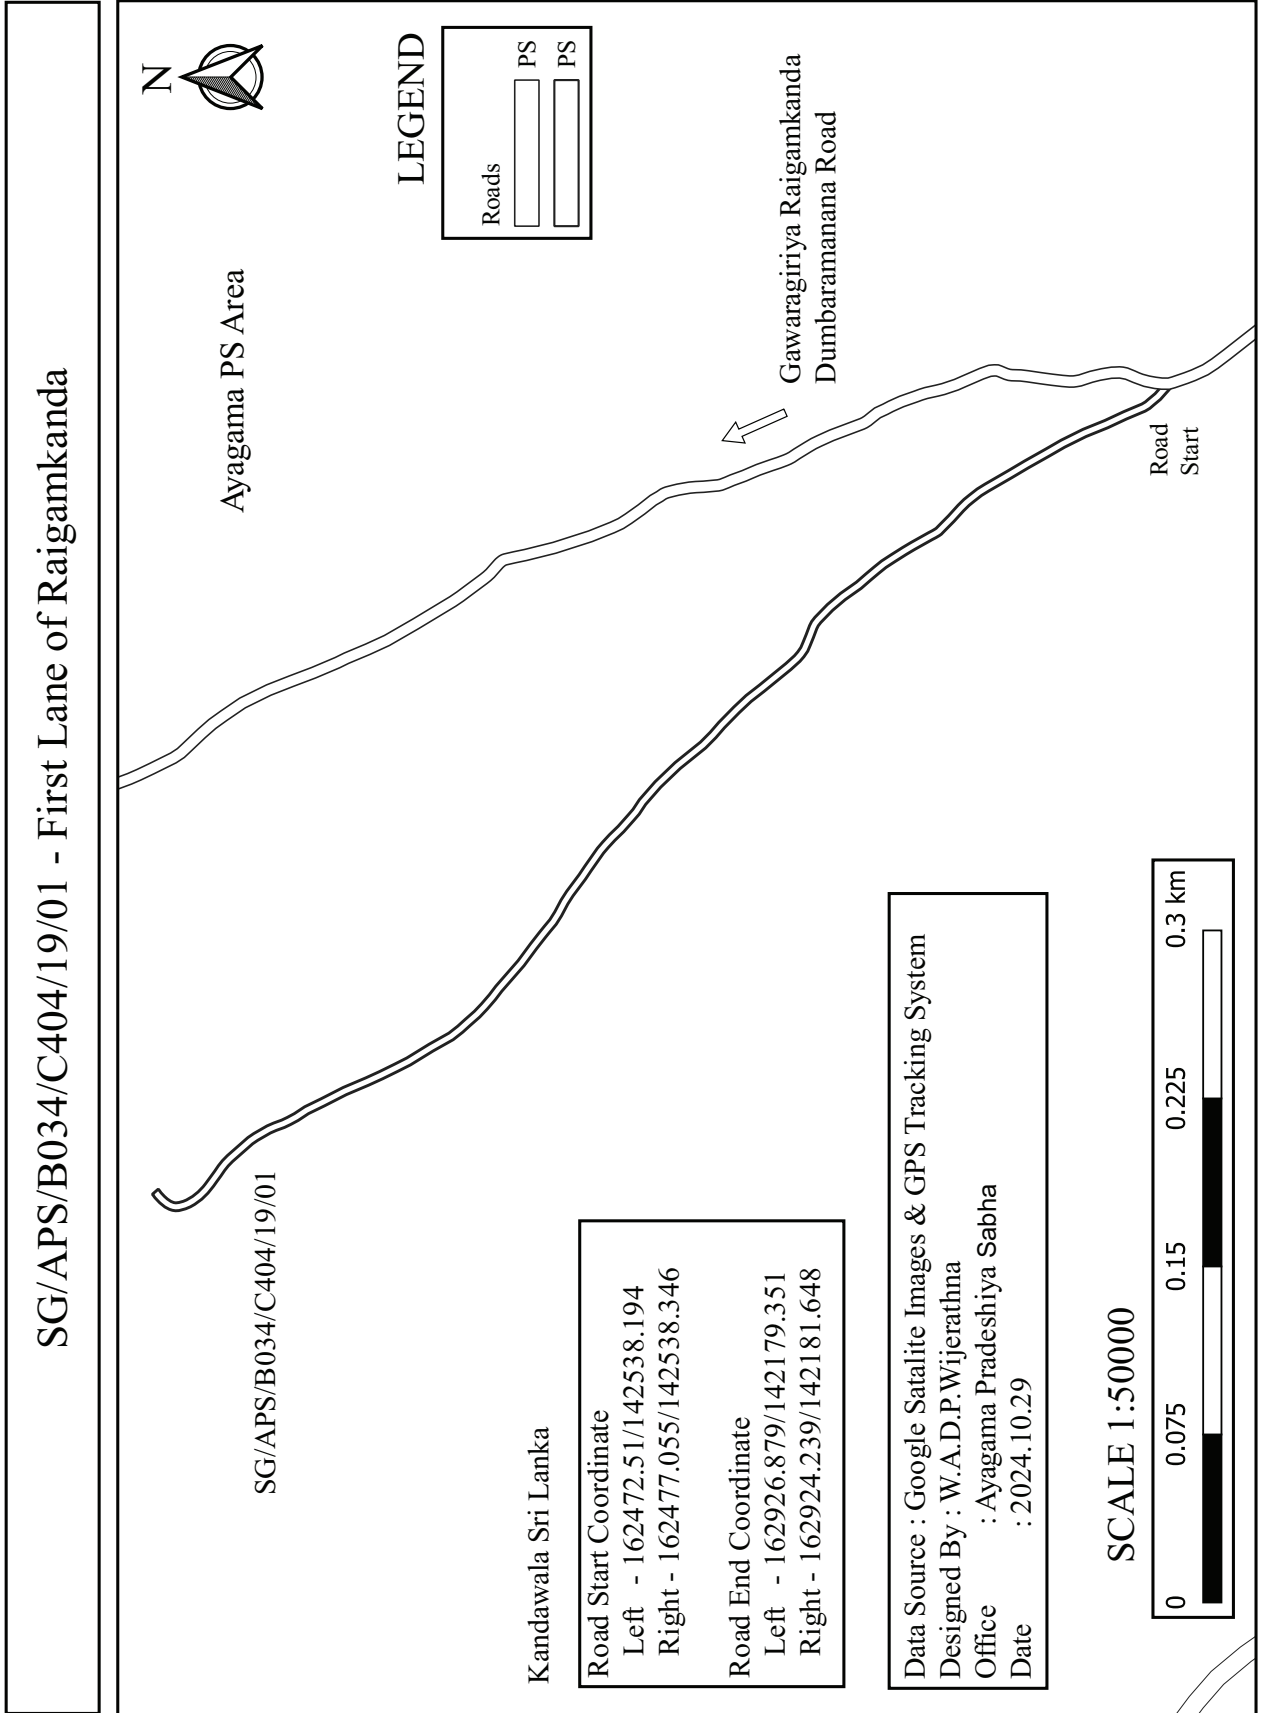


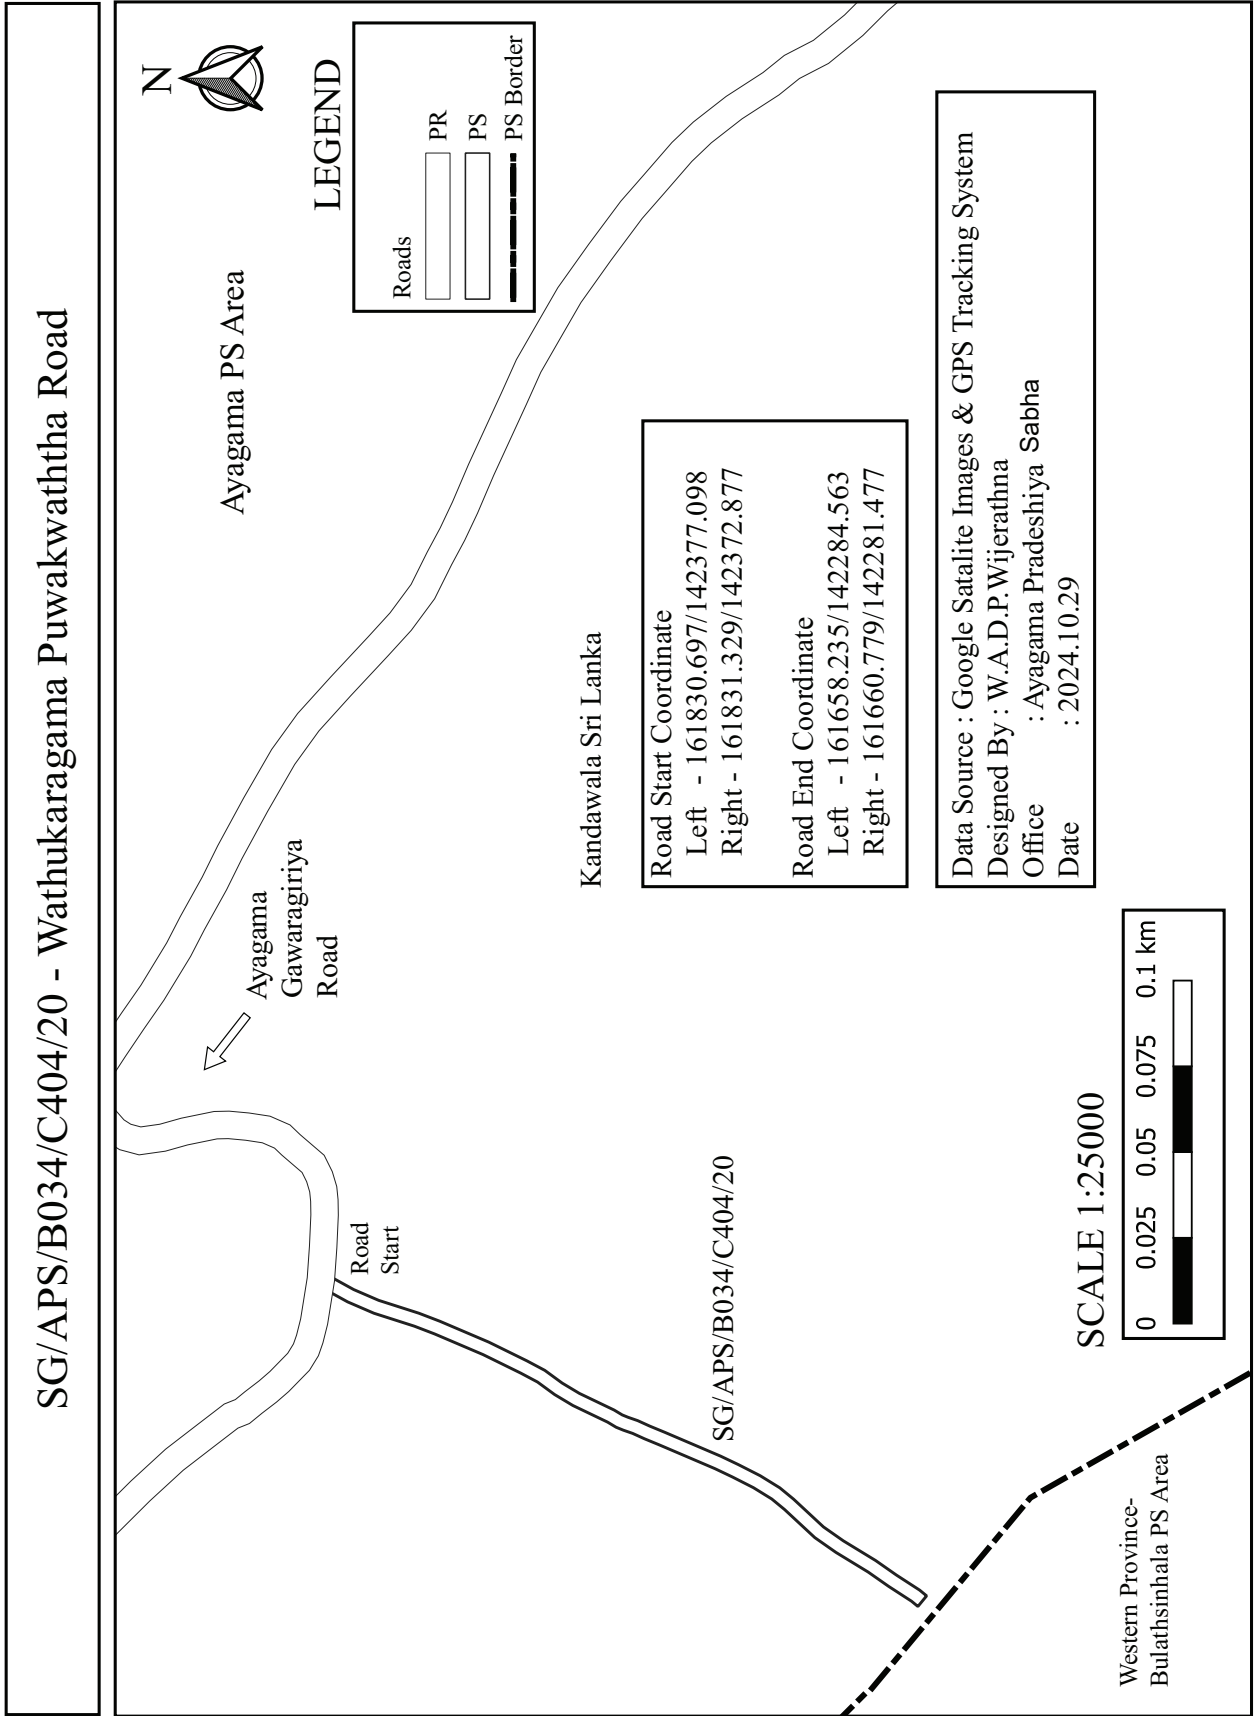



SG/APS/B034/C404/20/01 - Wathukaragama Galwaththa Road

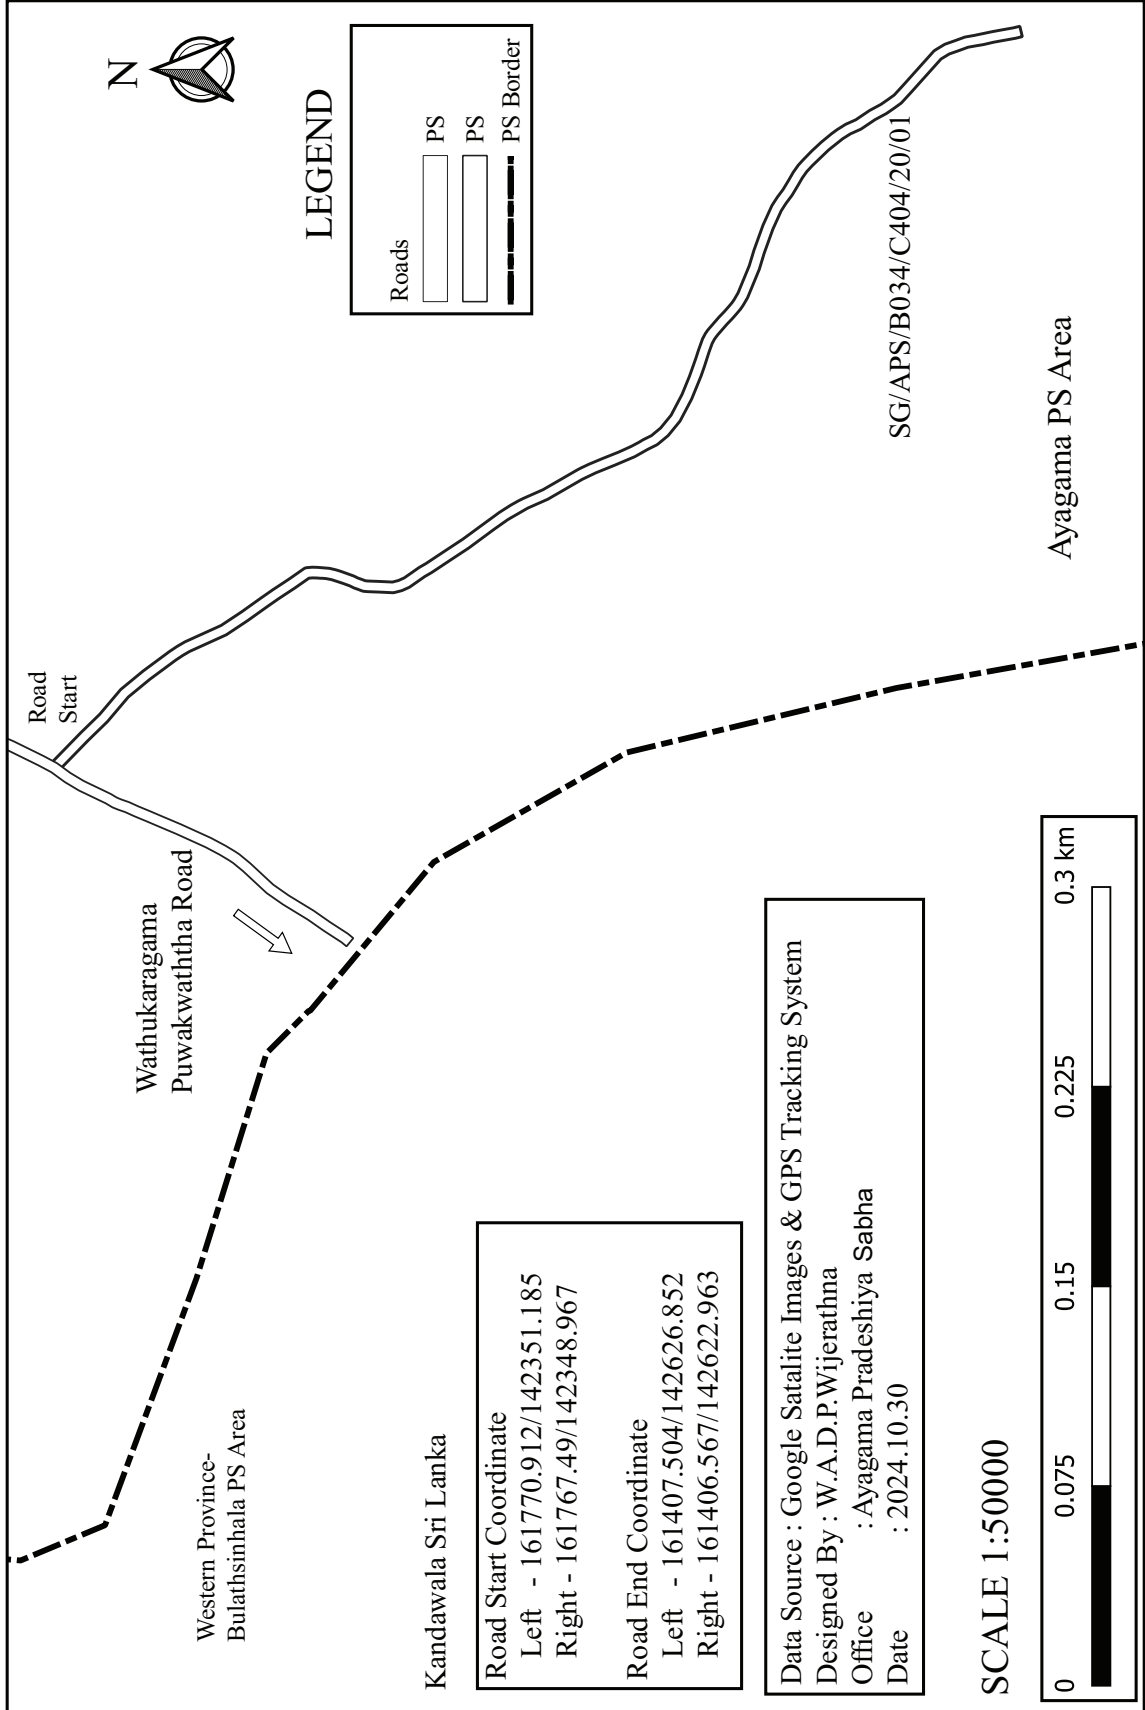


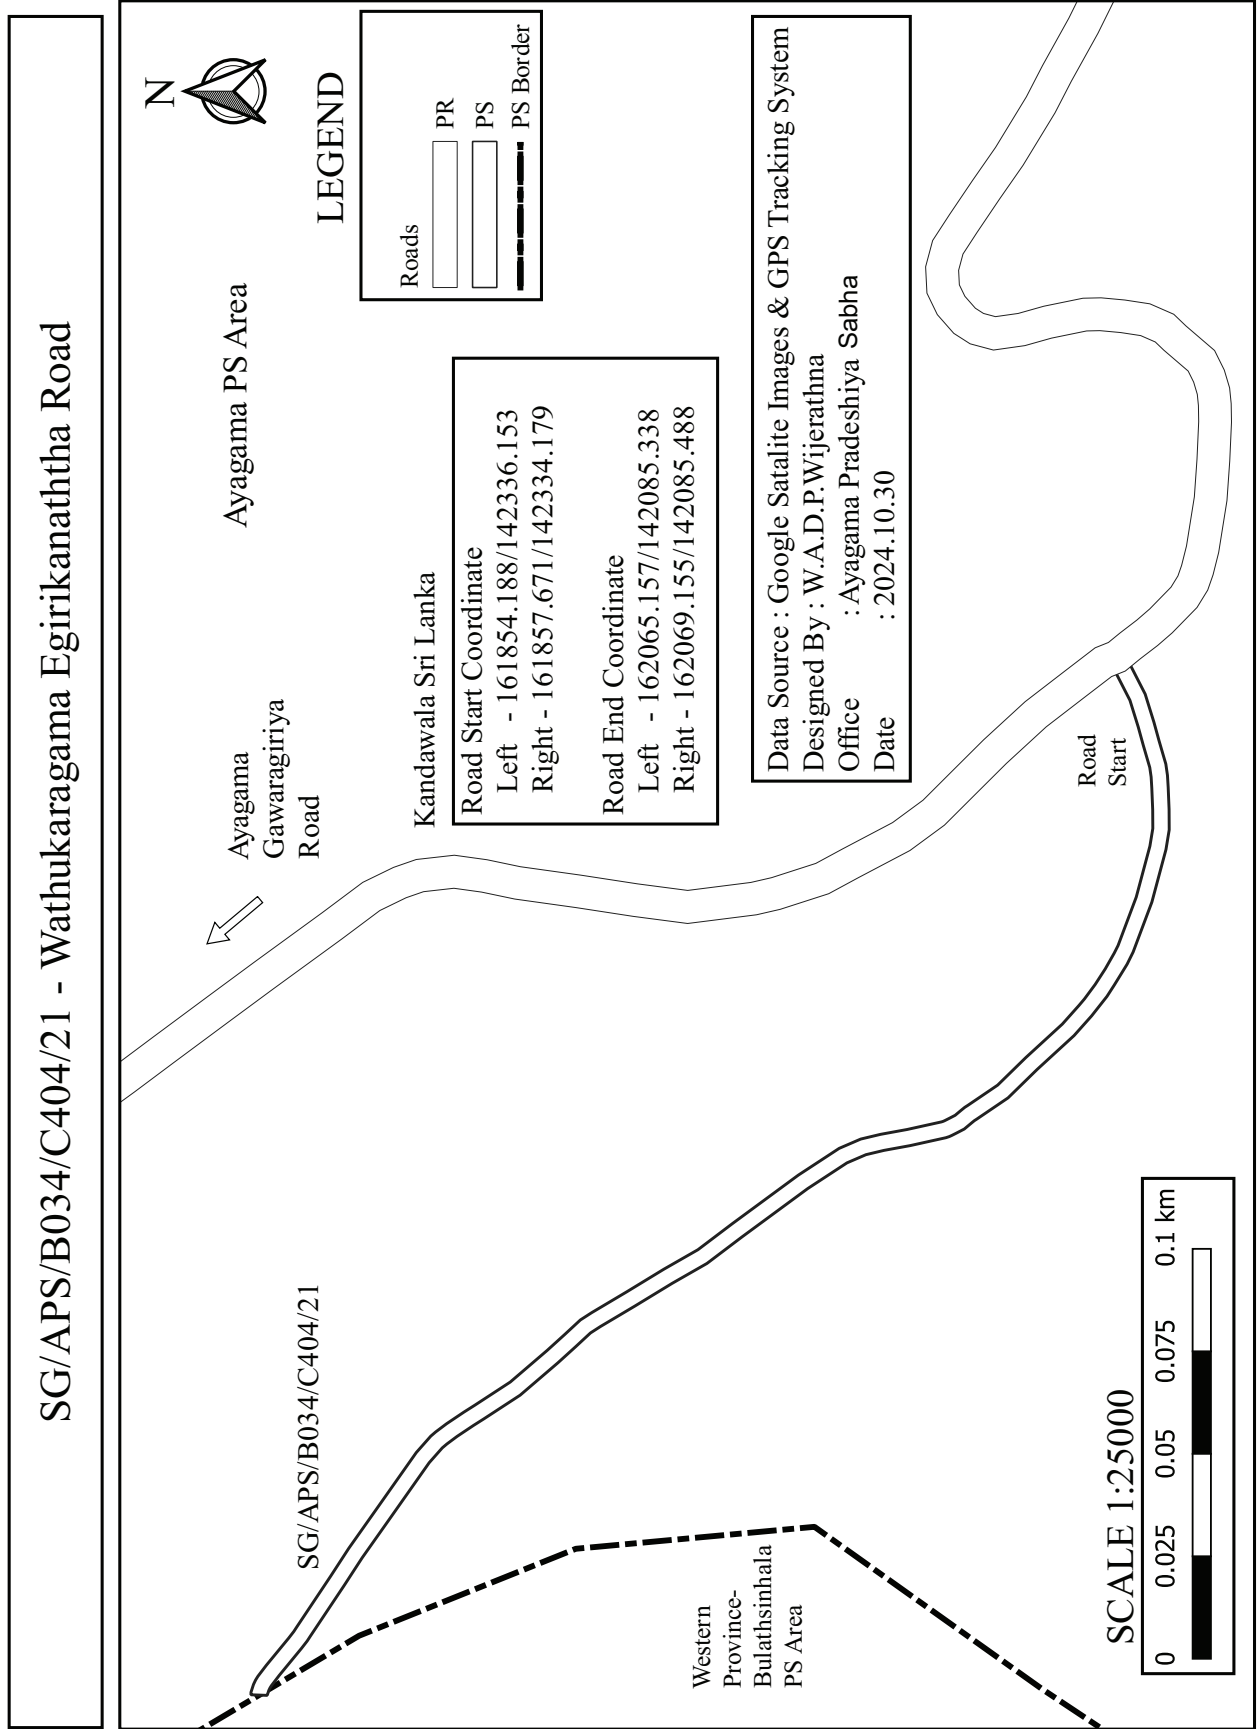


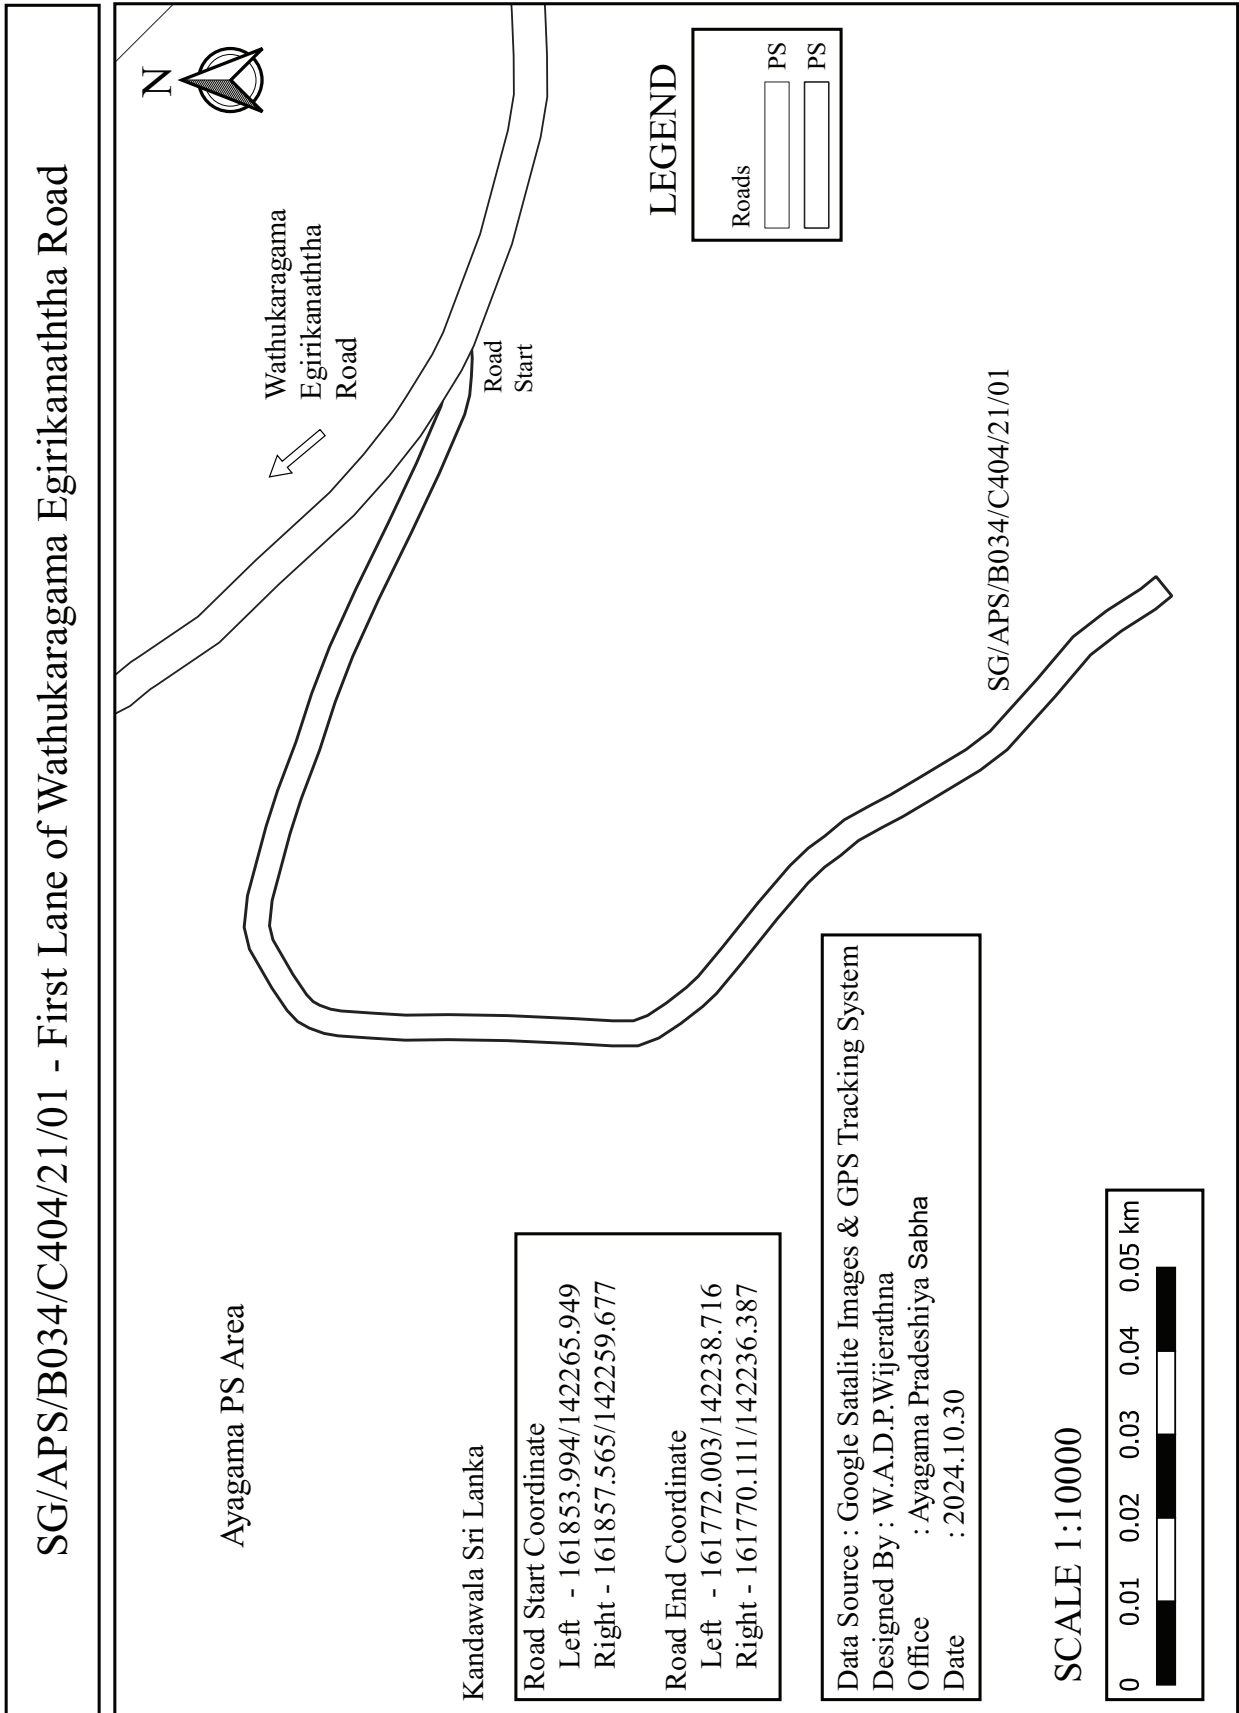


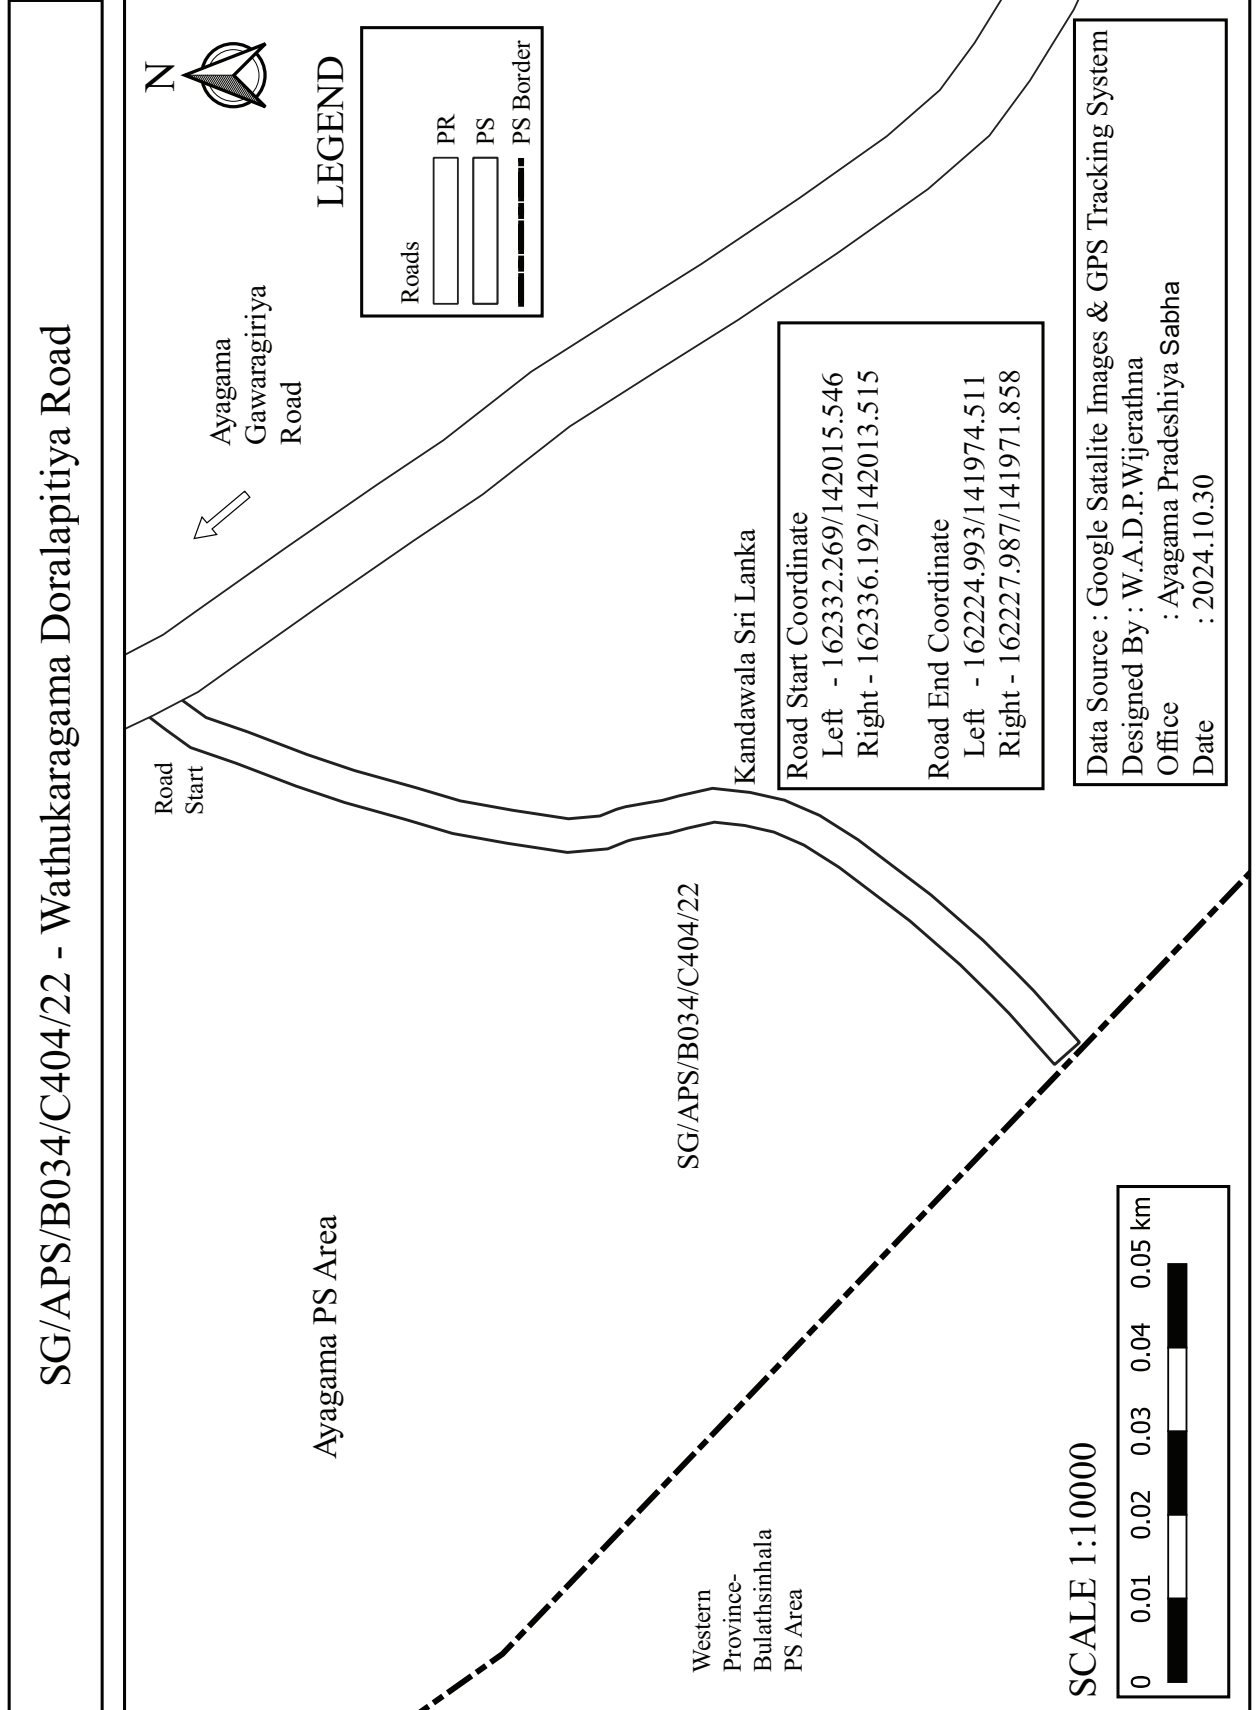


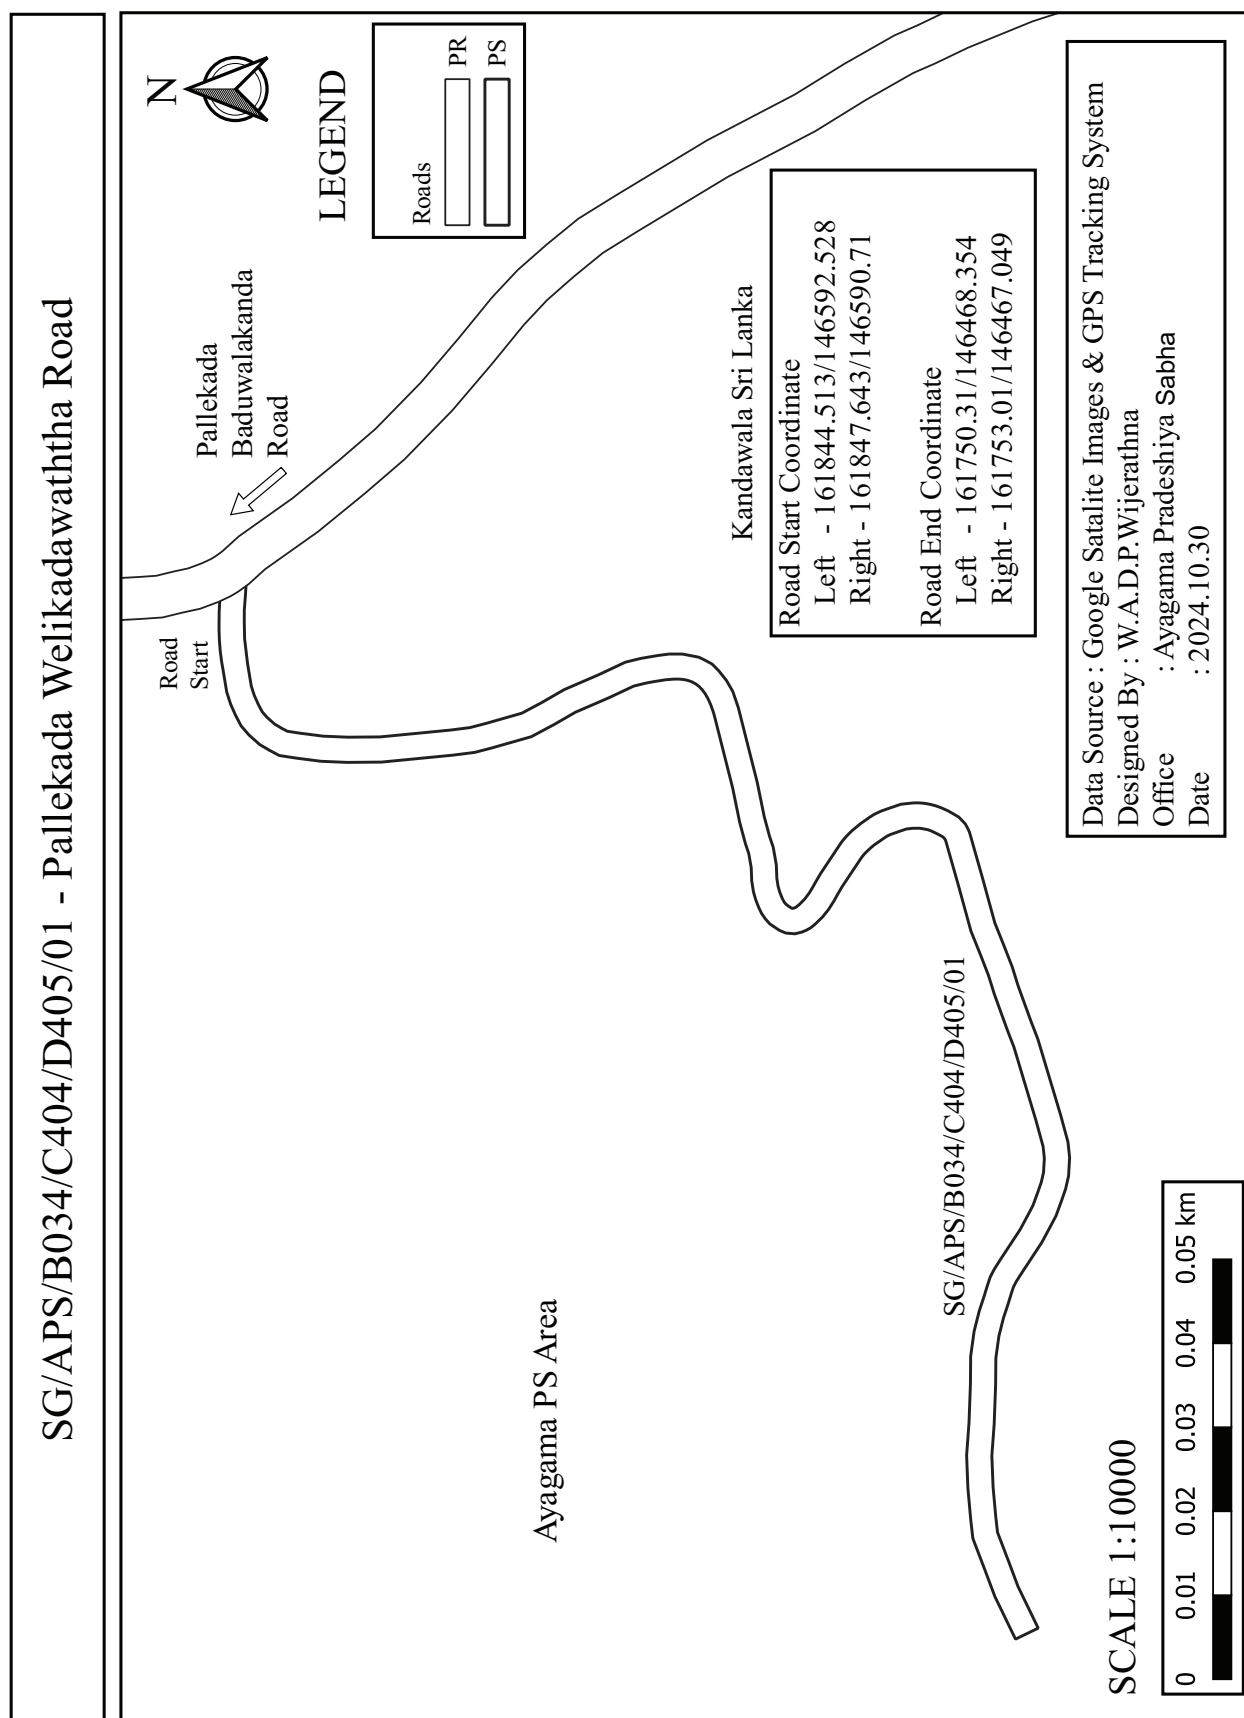


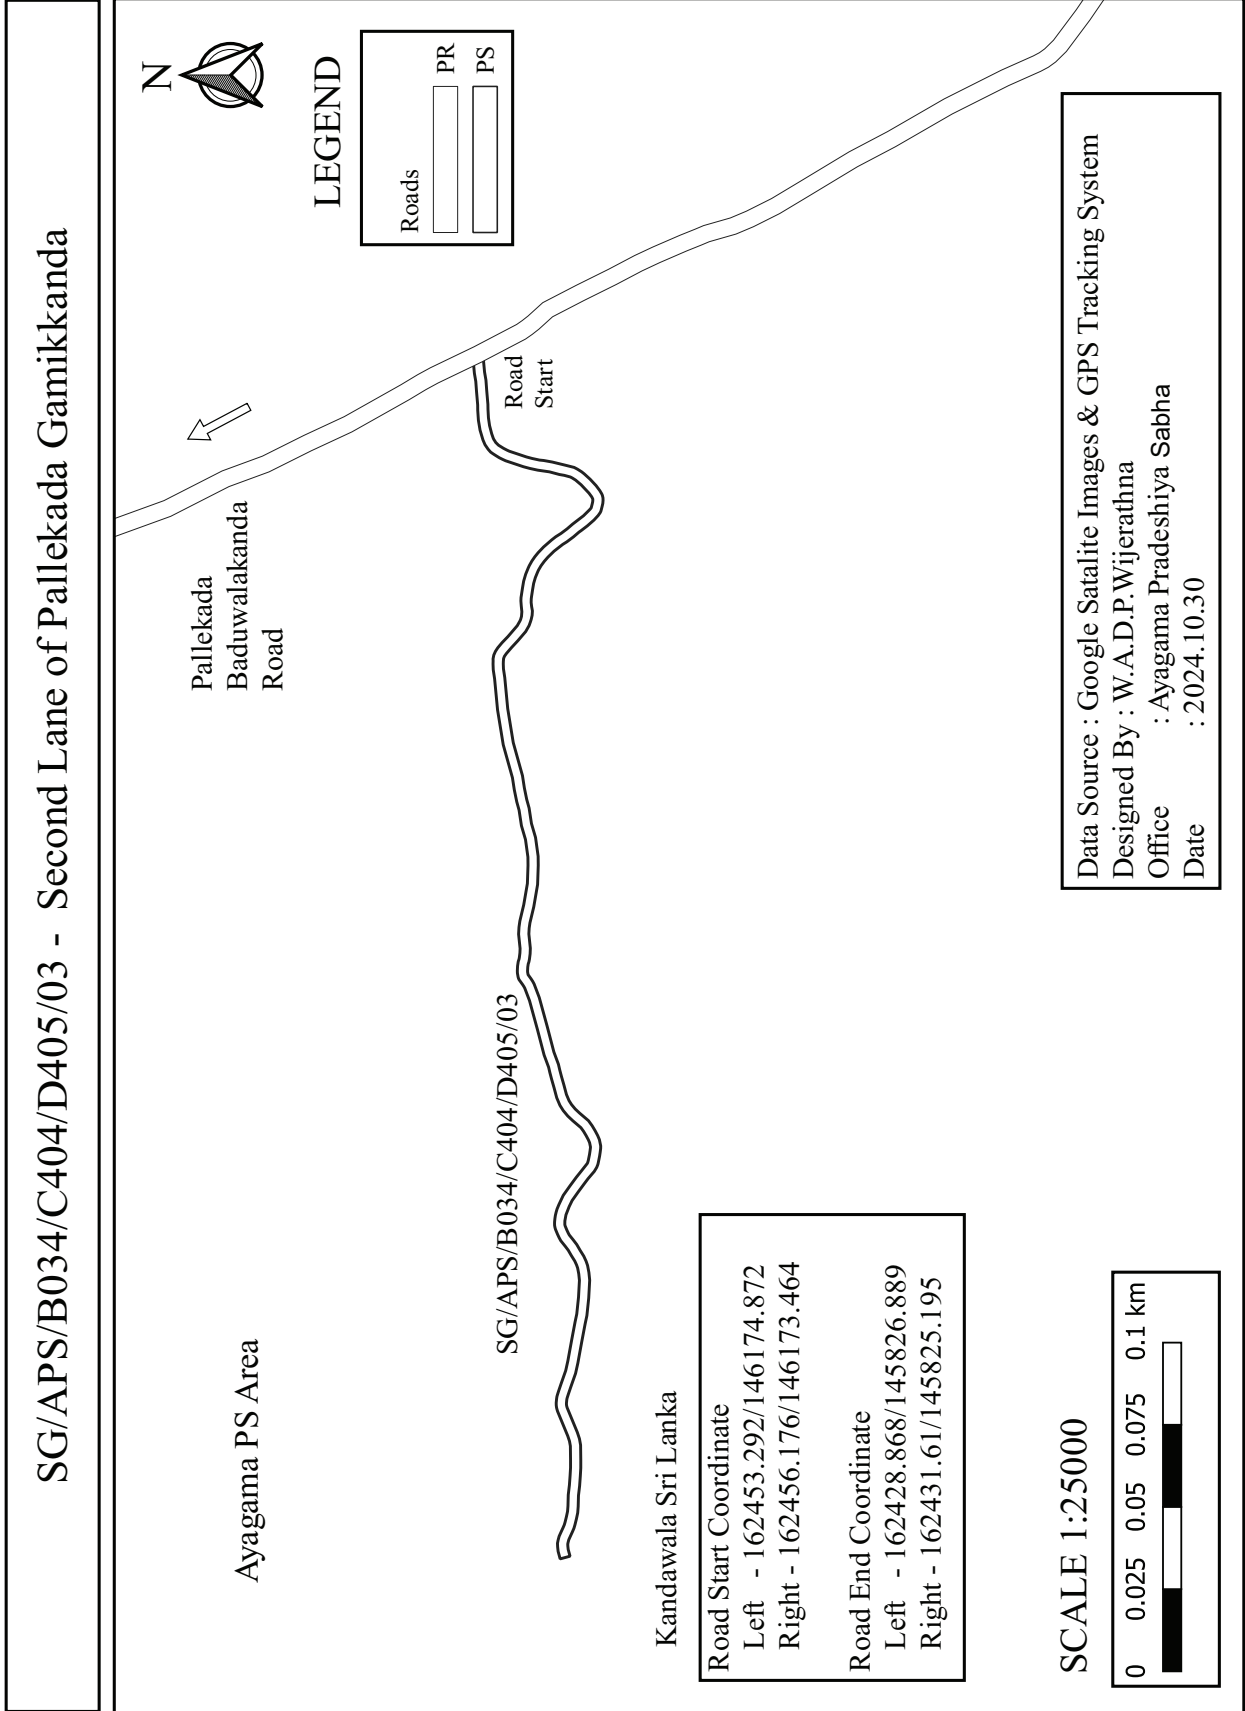


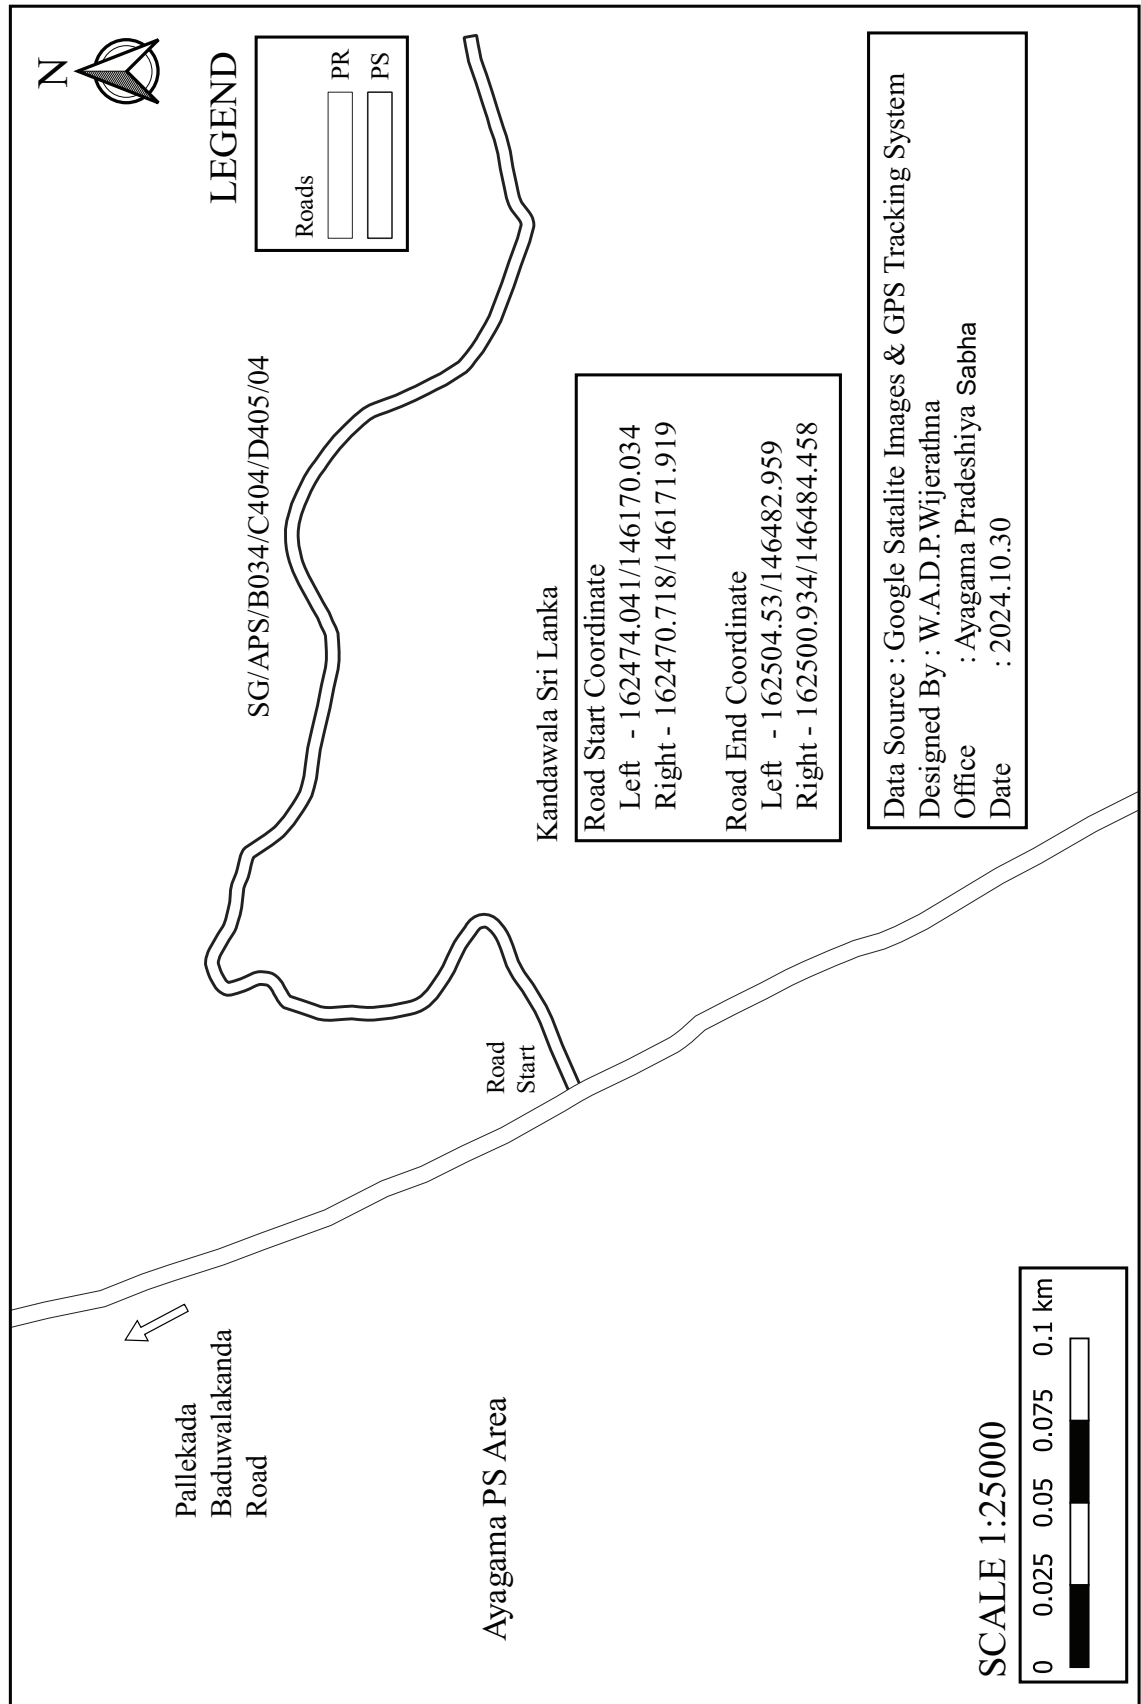


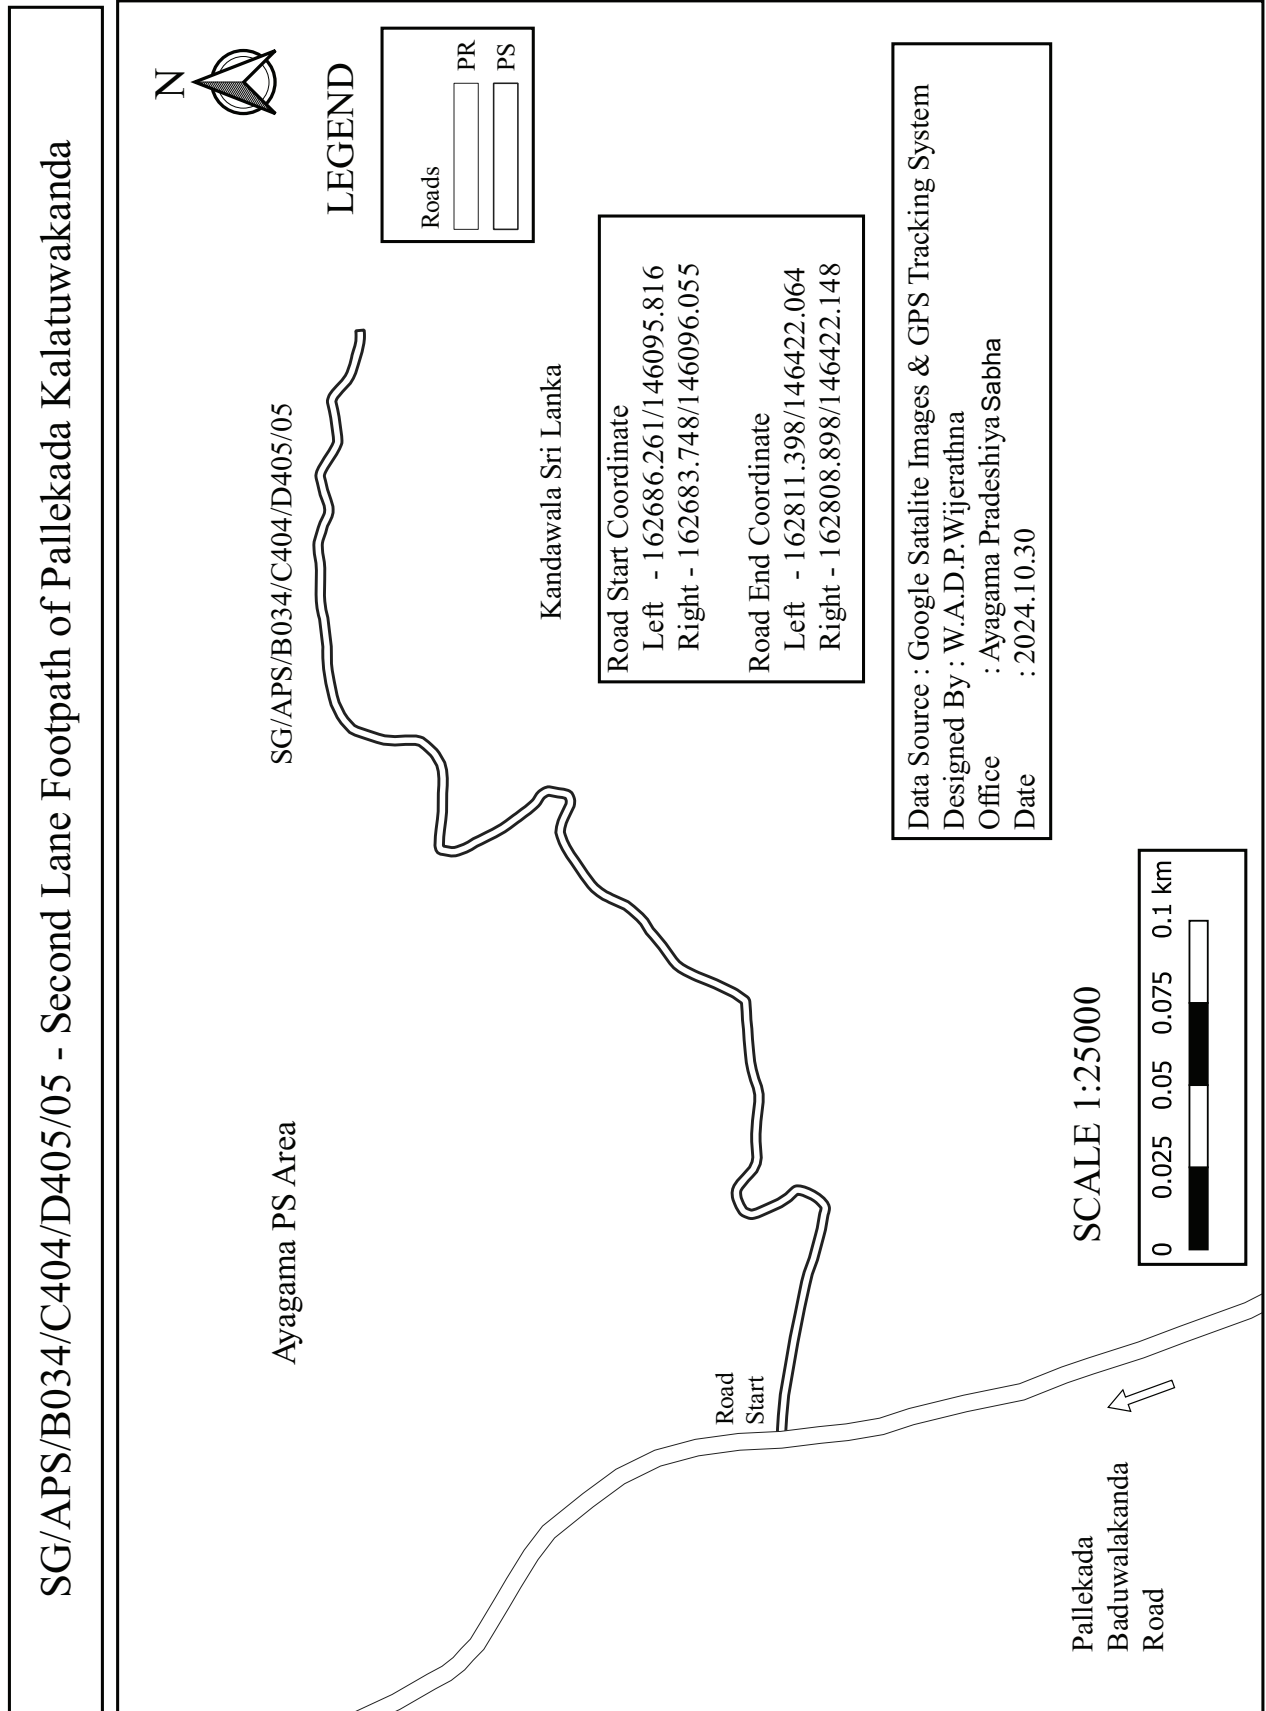


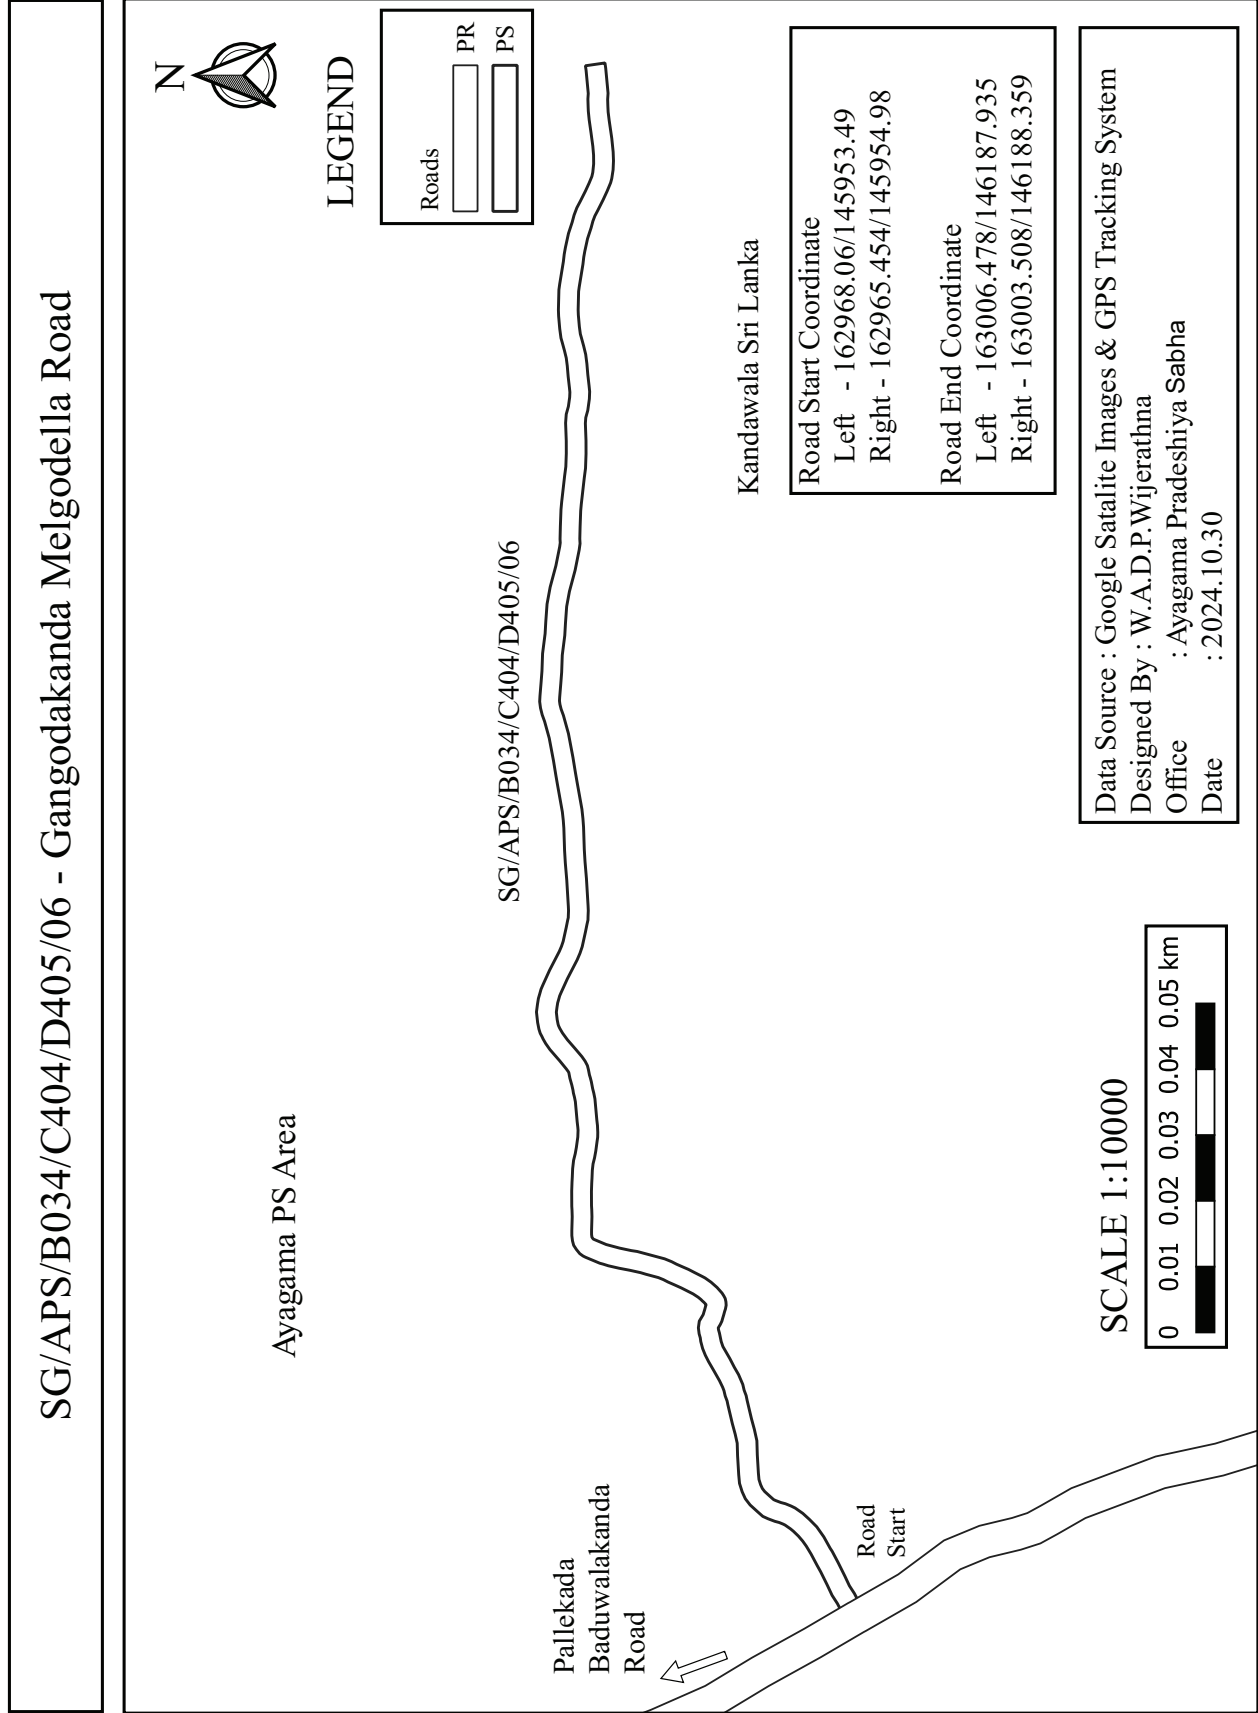


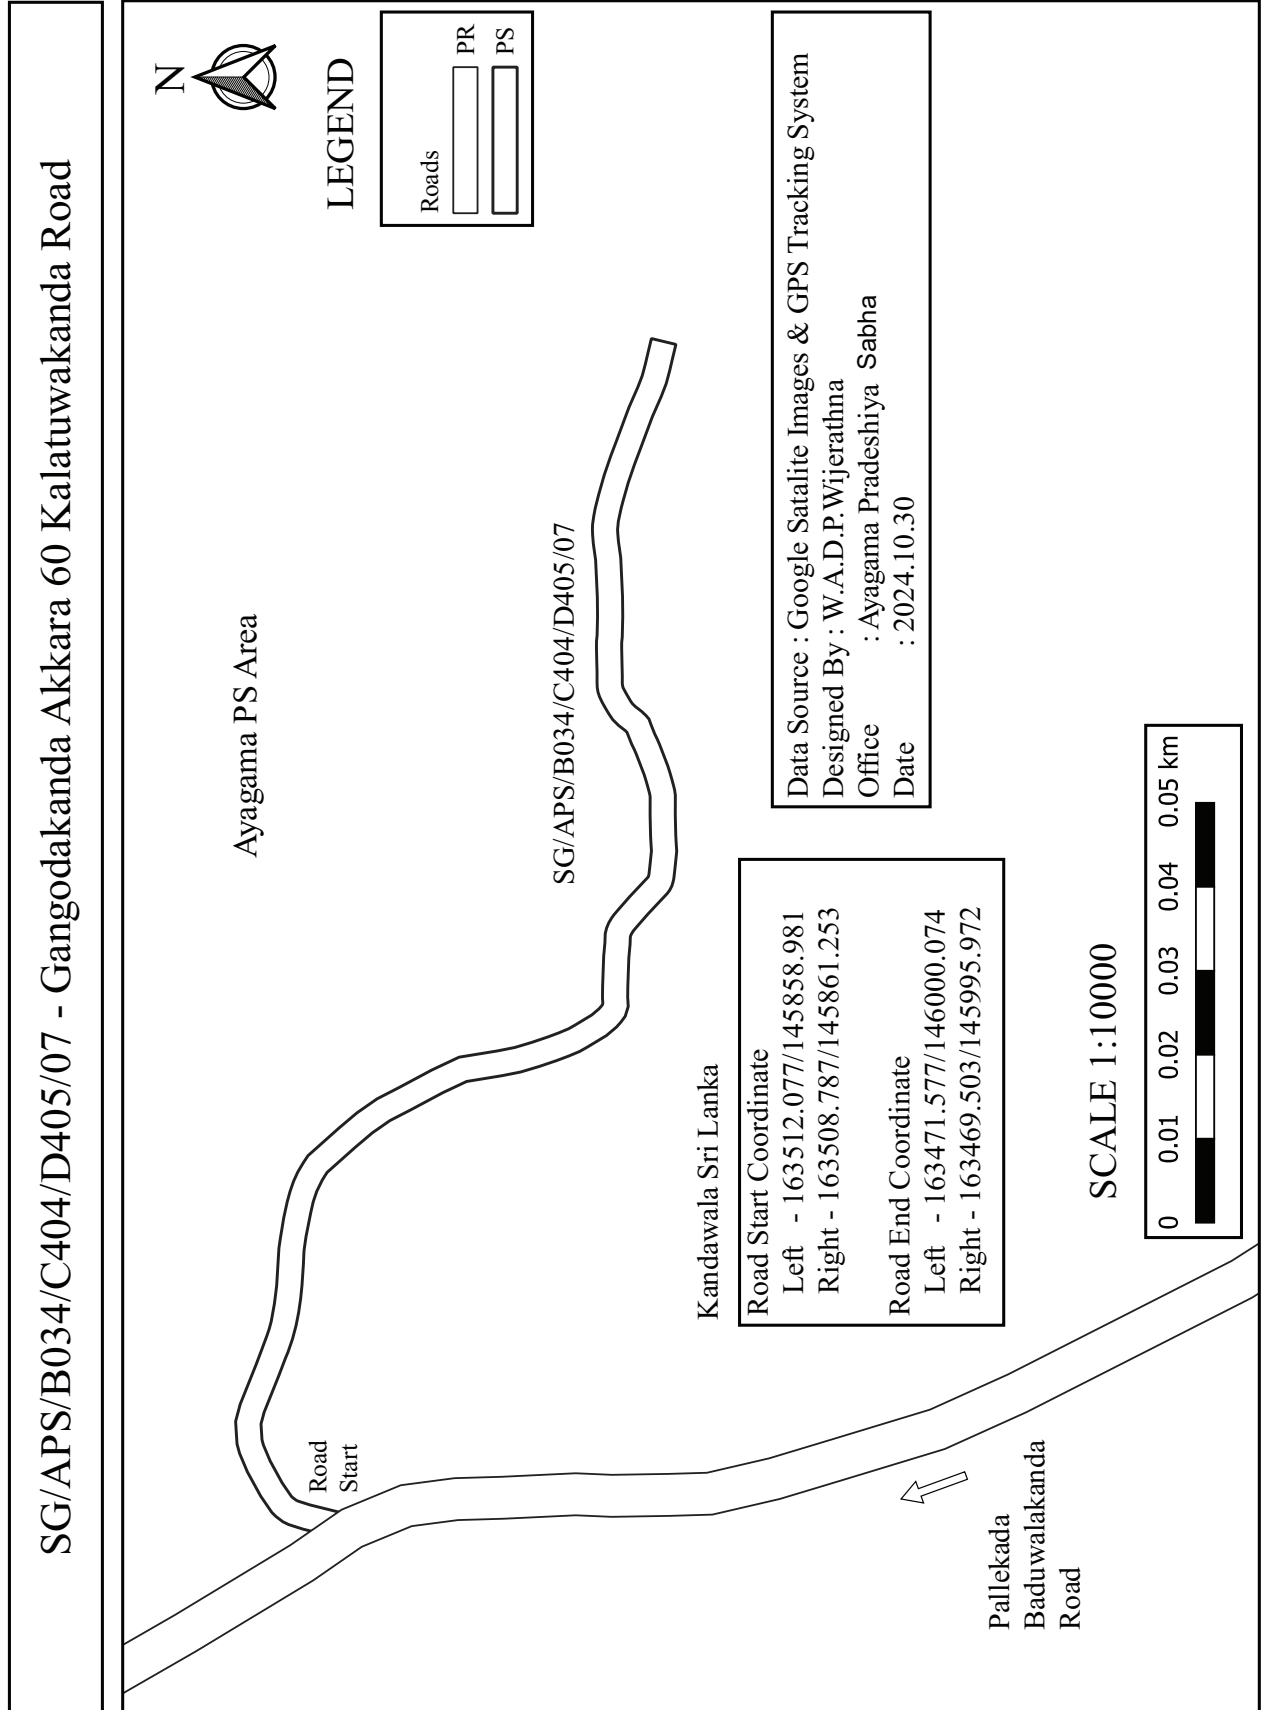


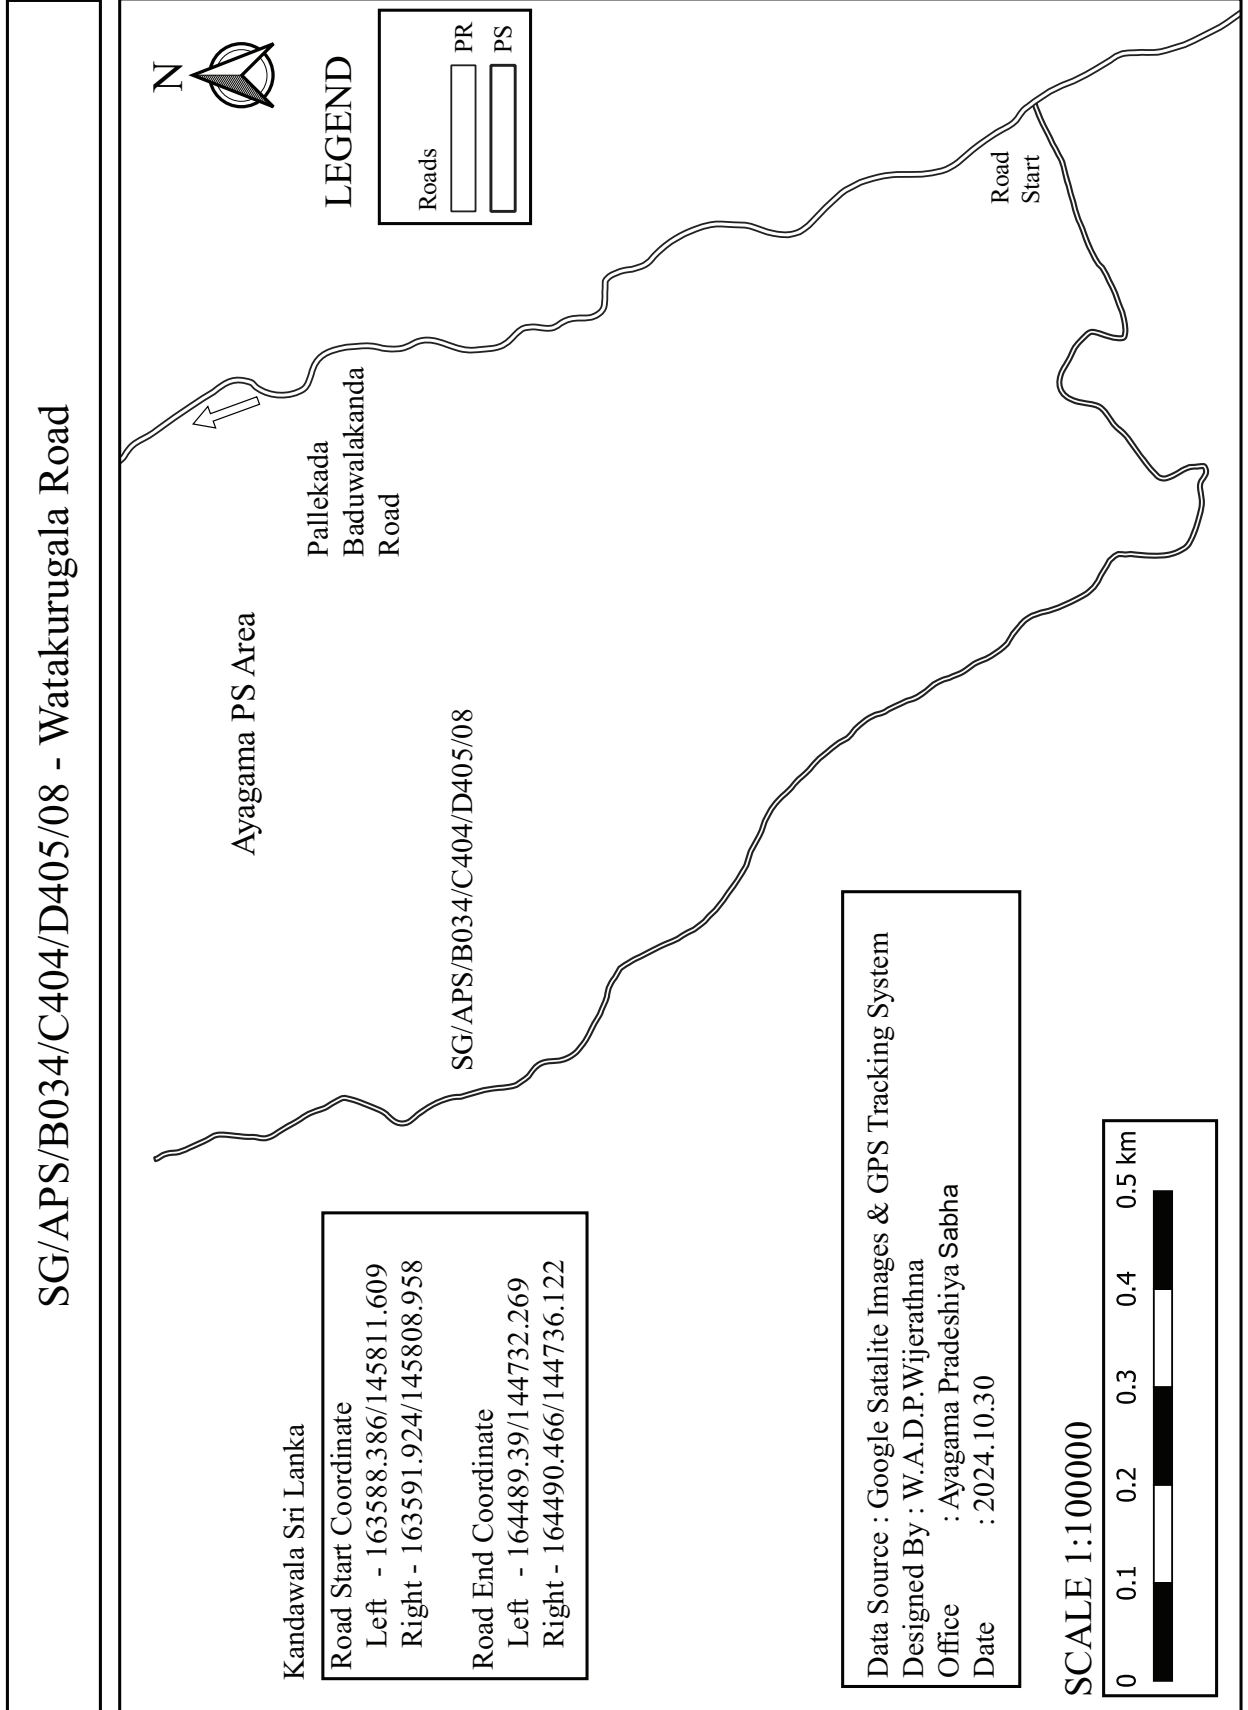


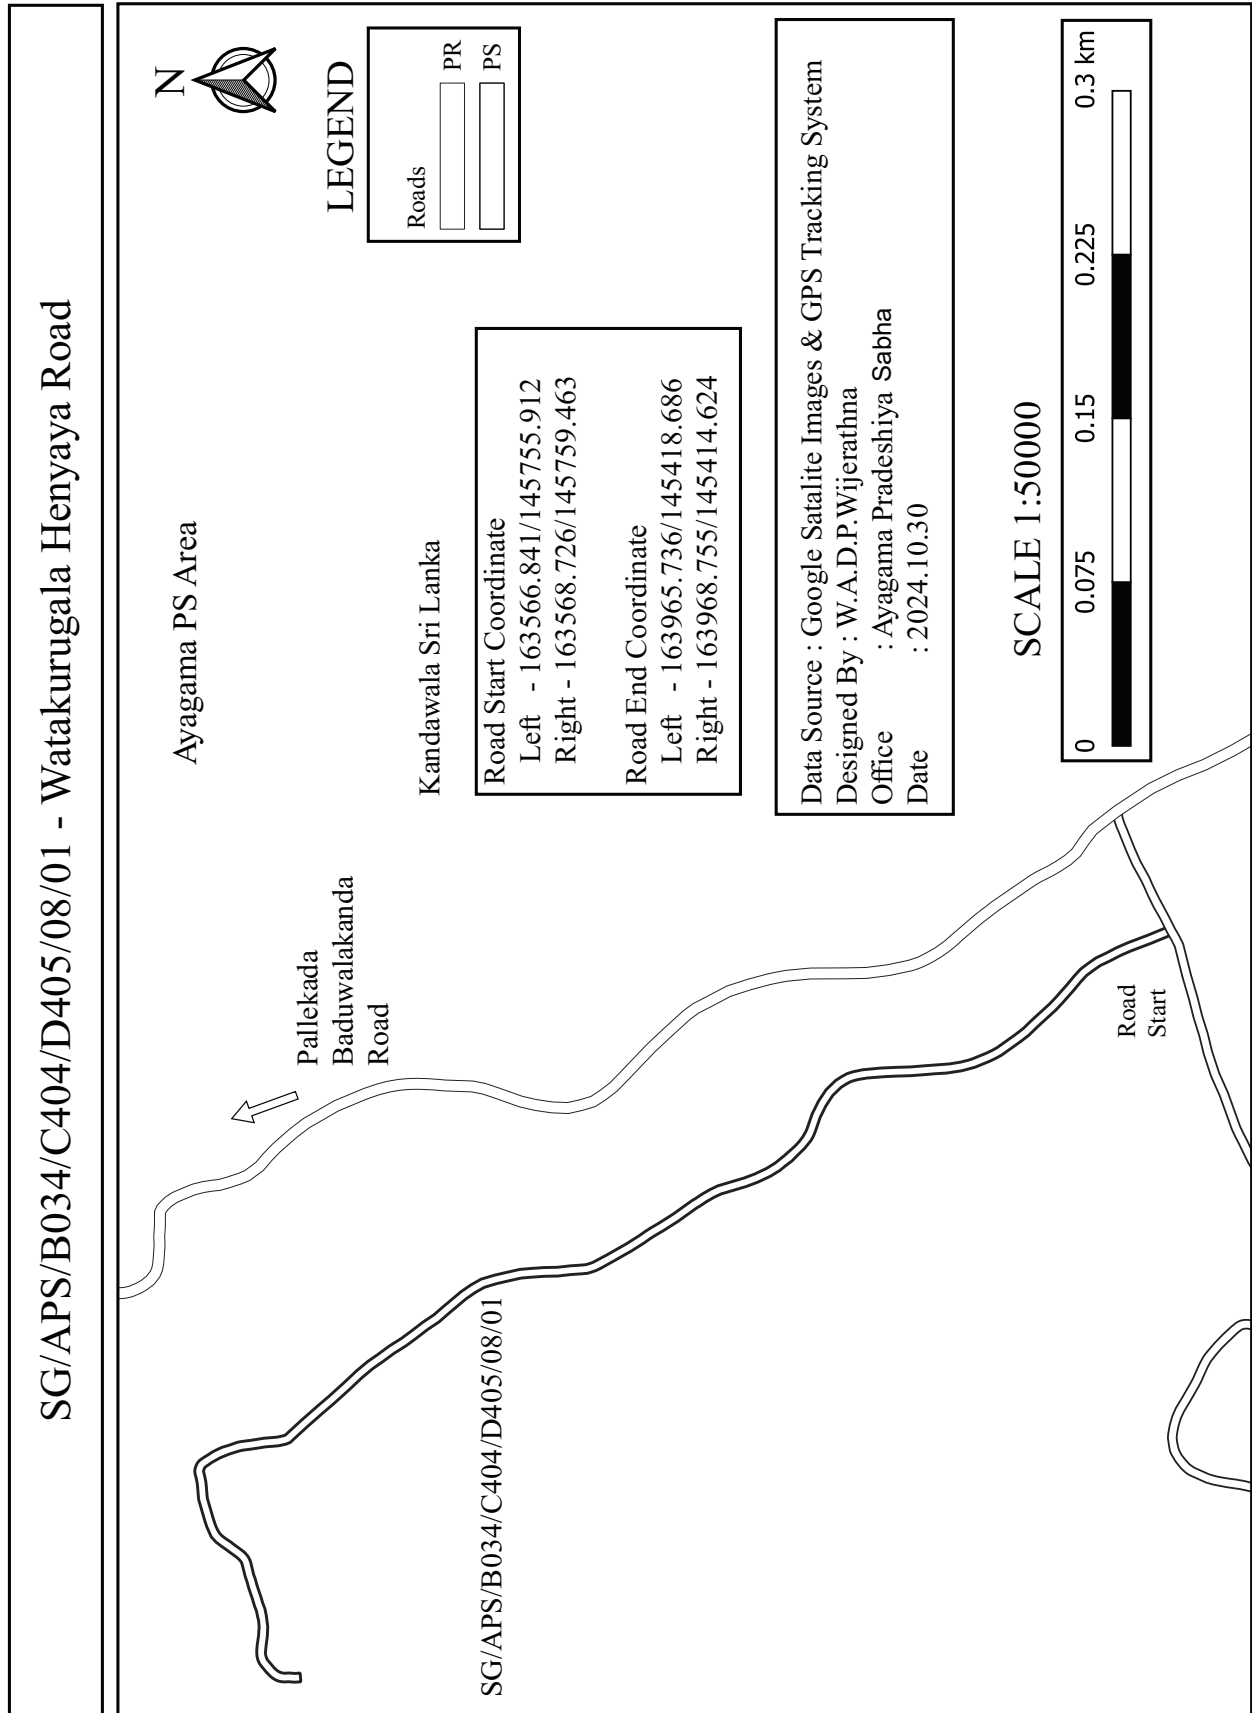


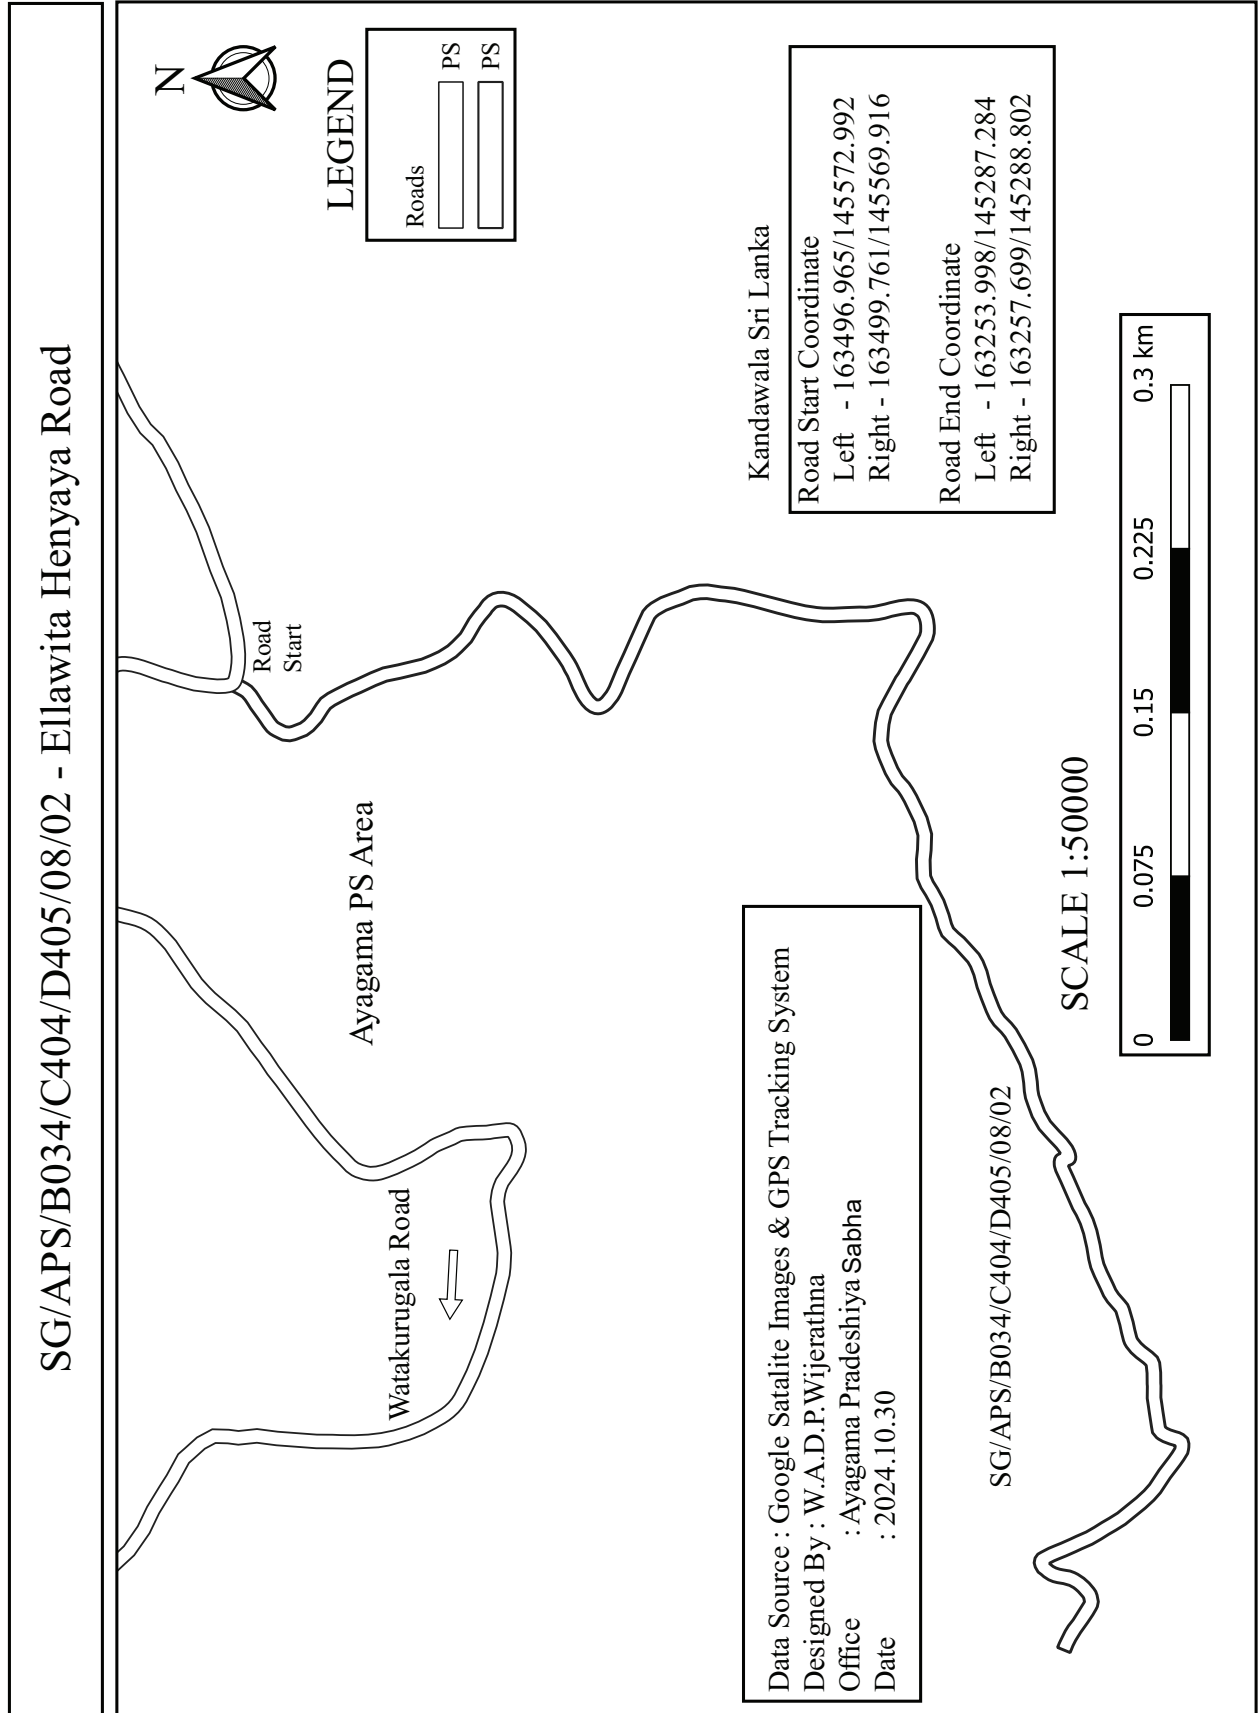


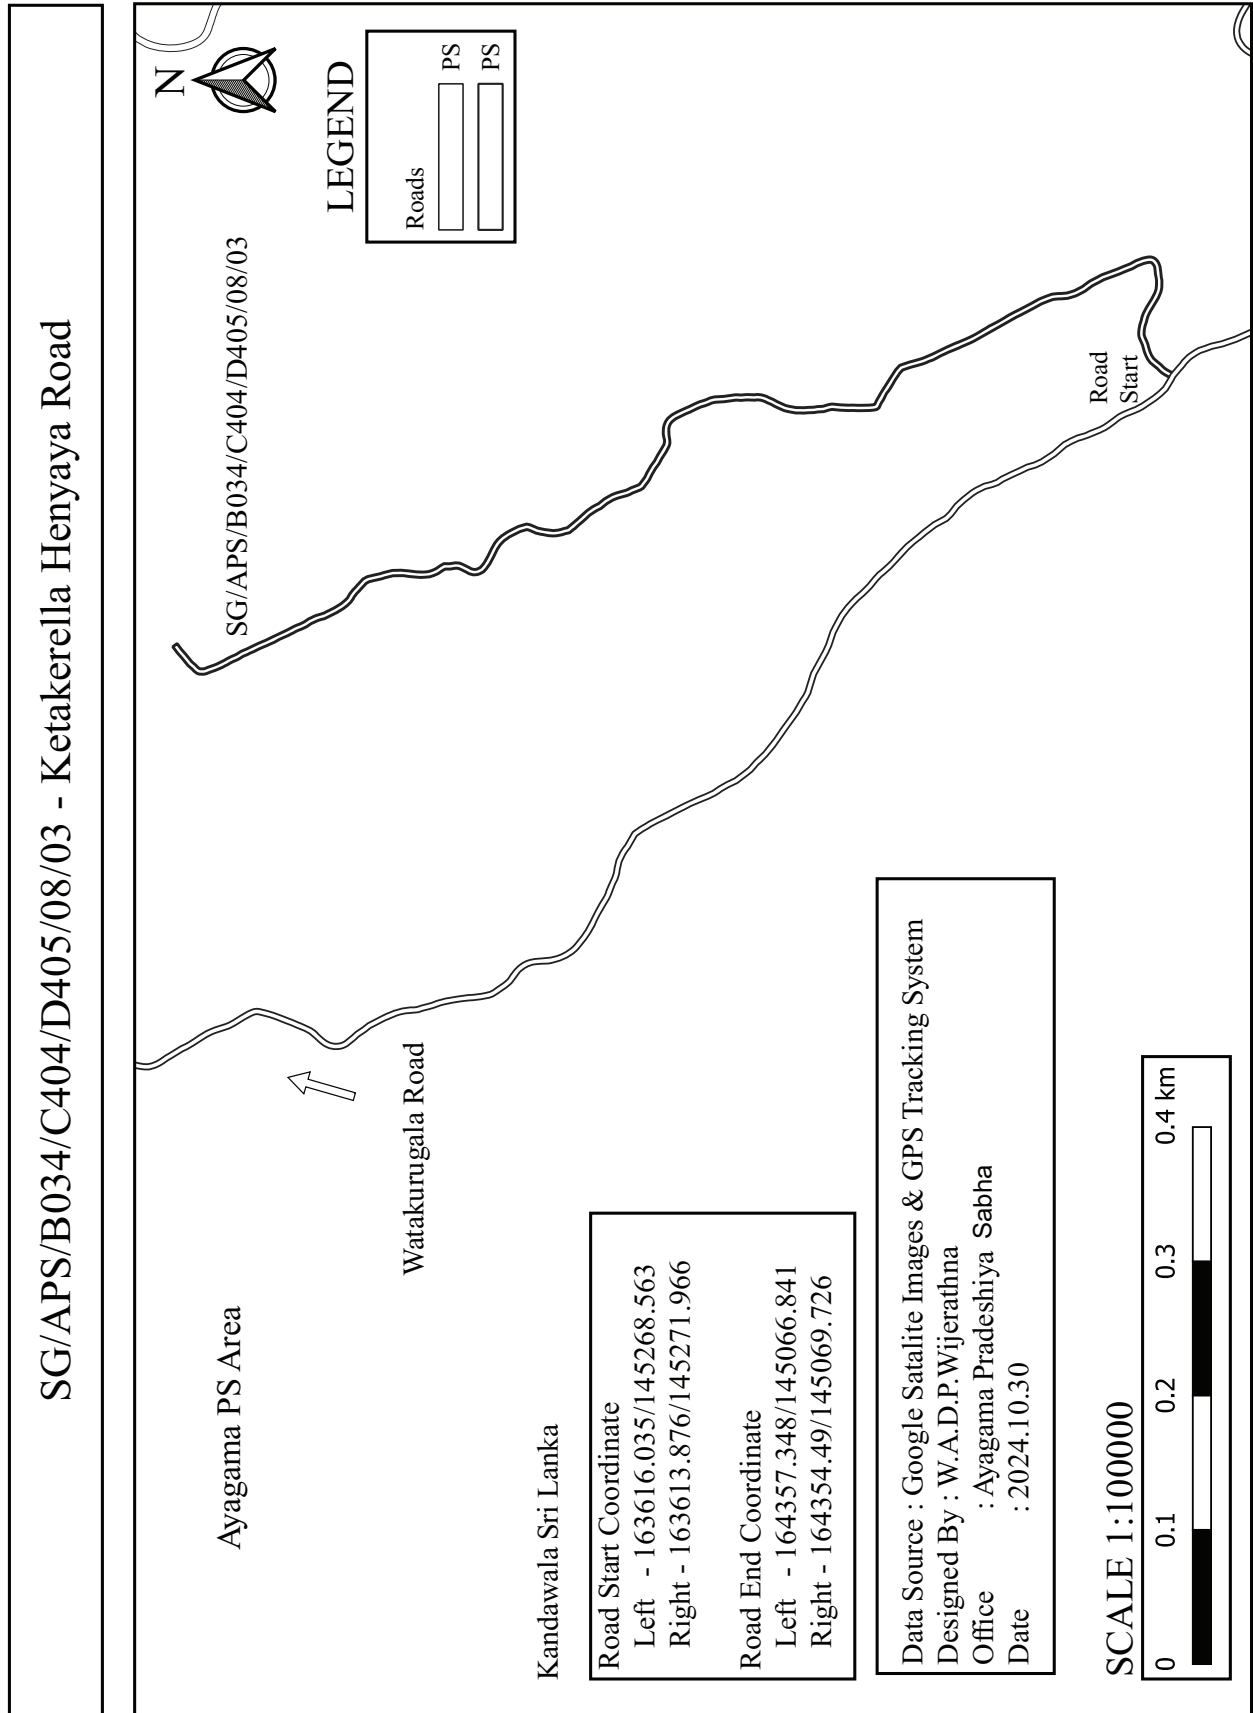


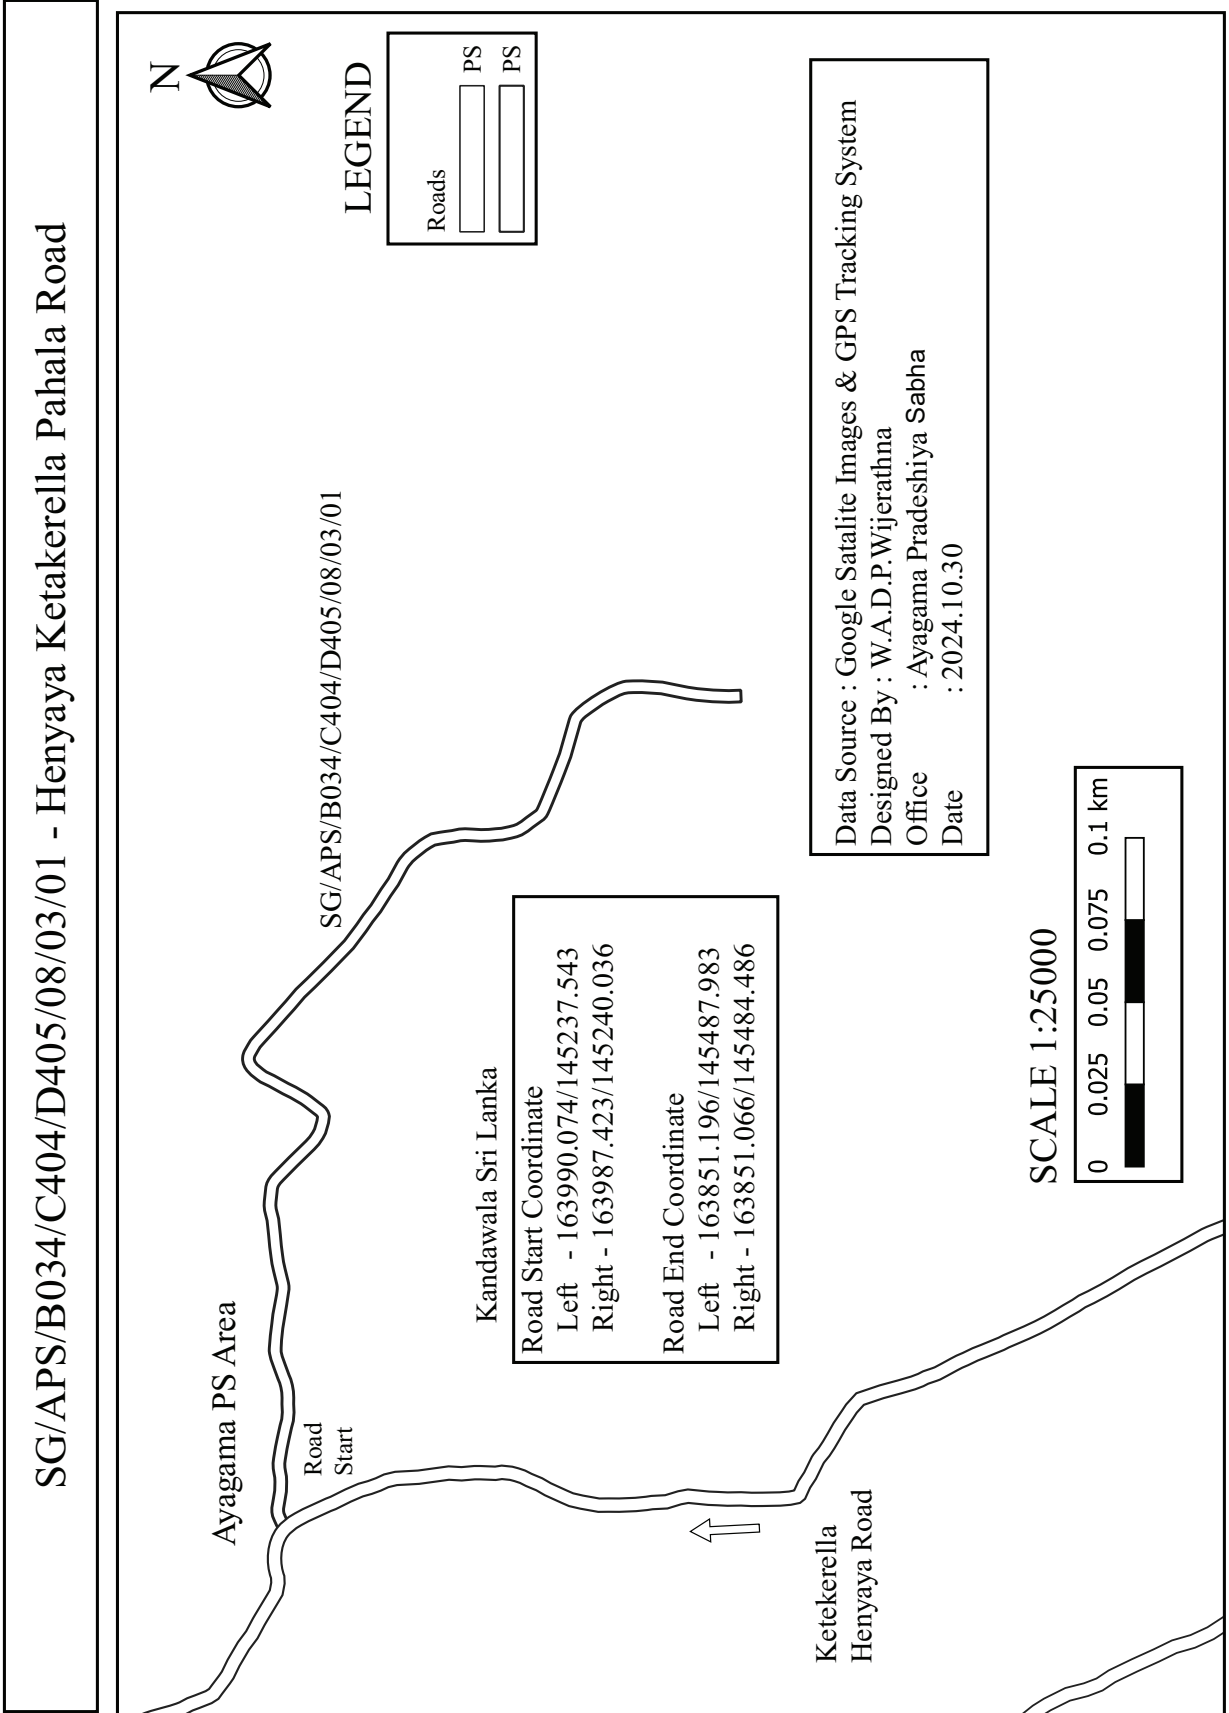


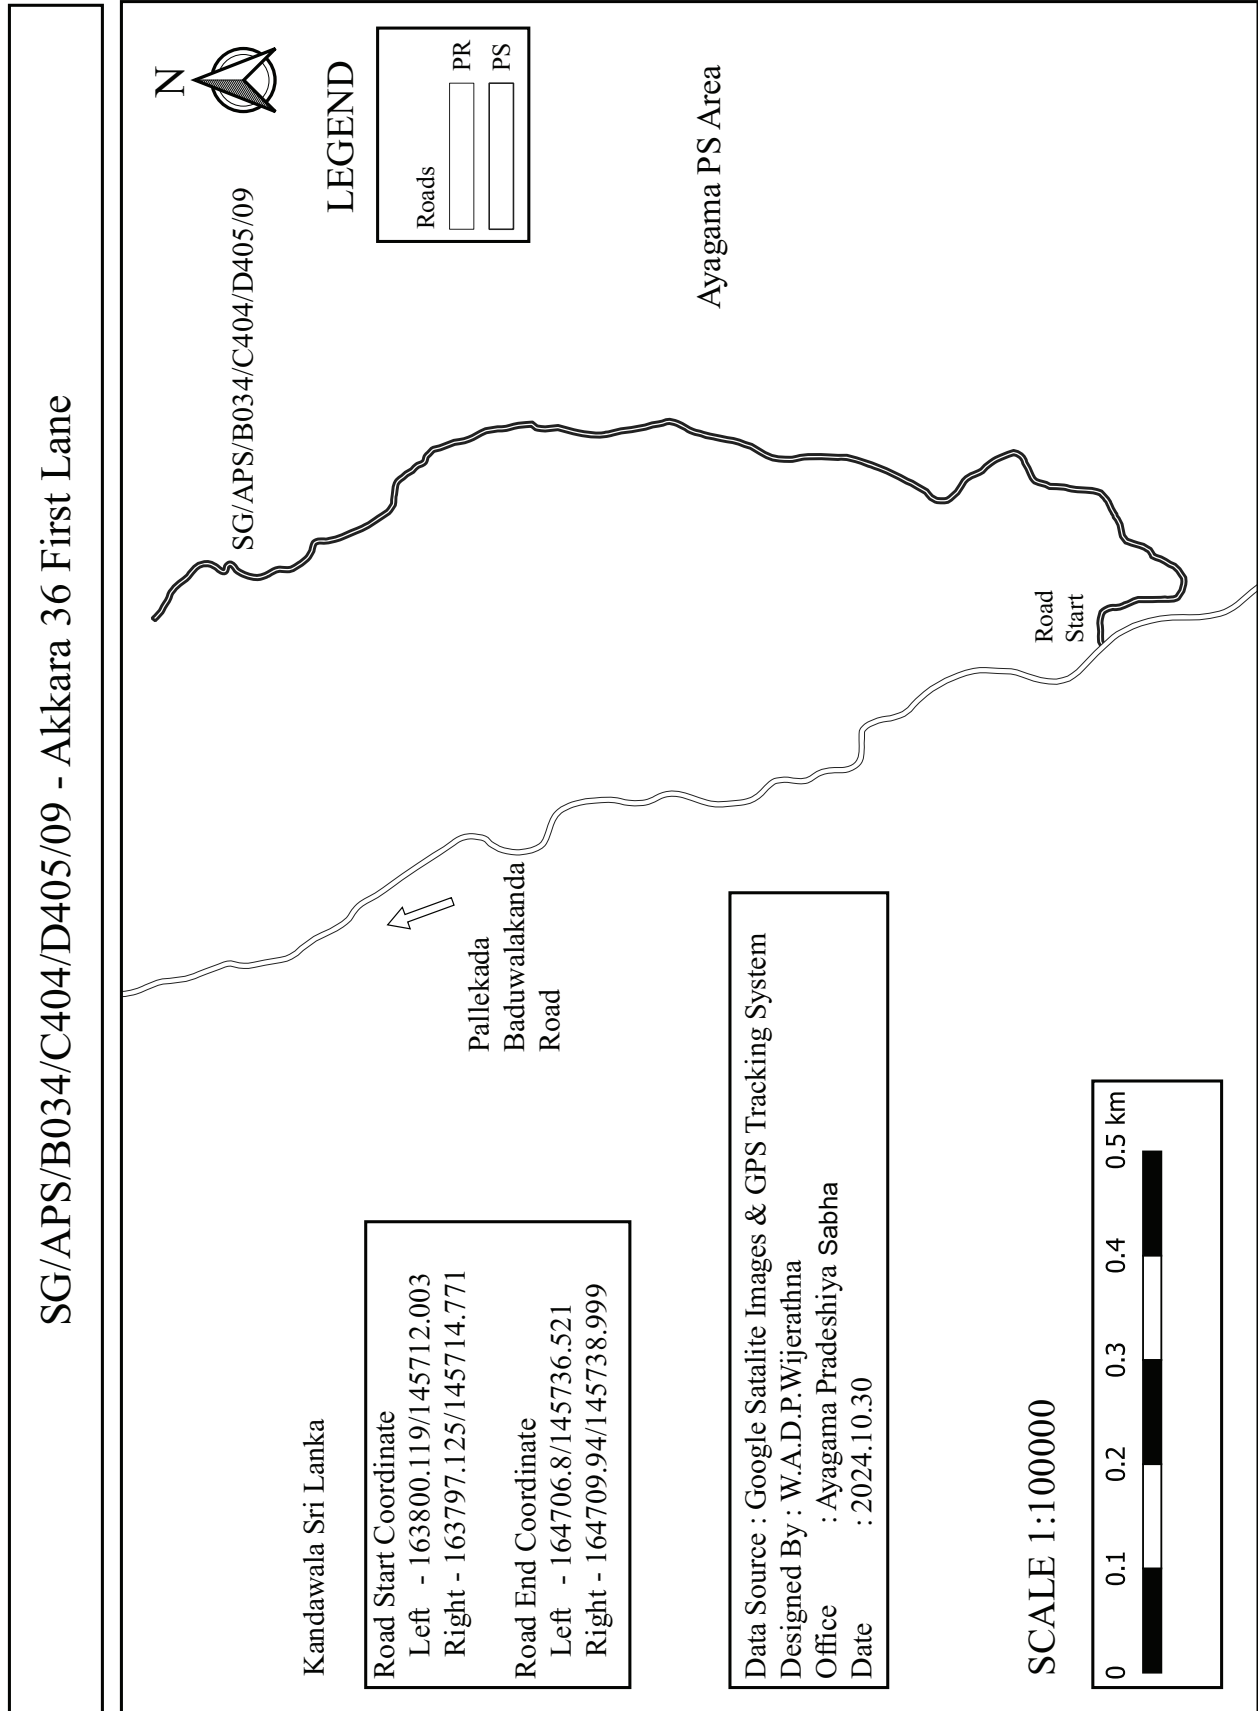


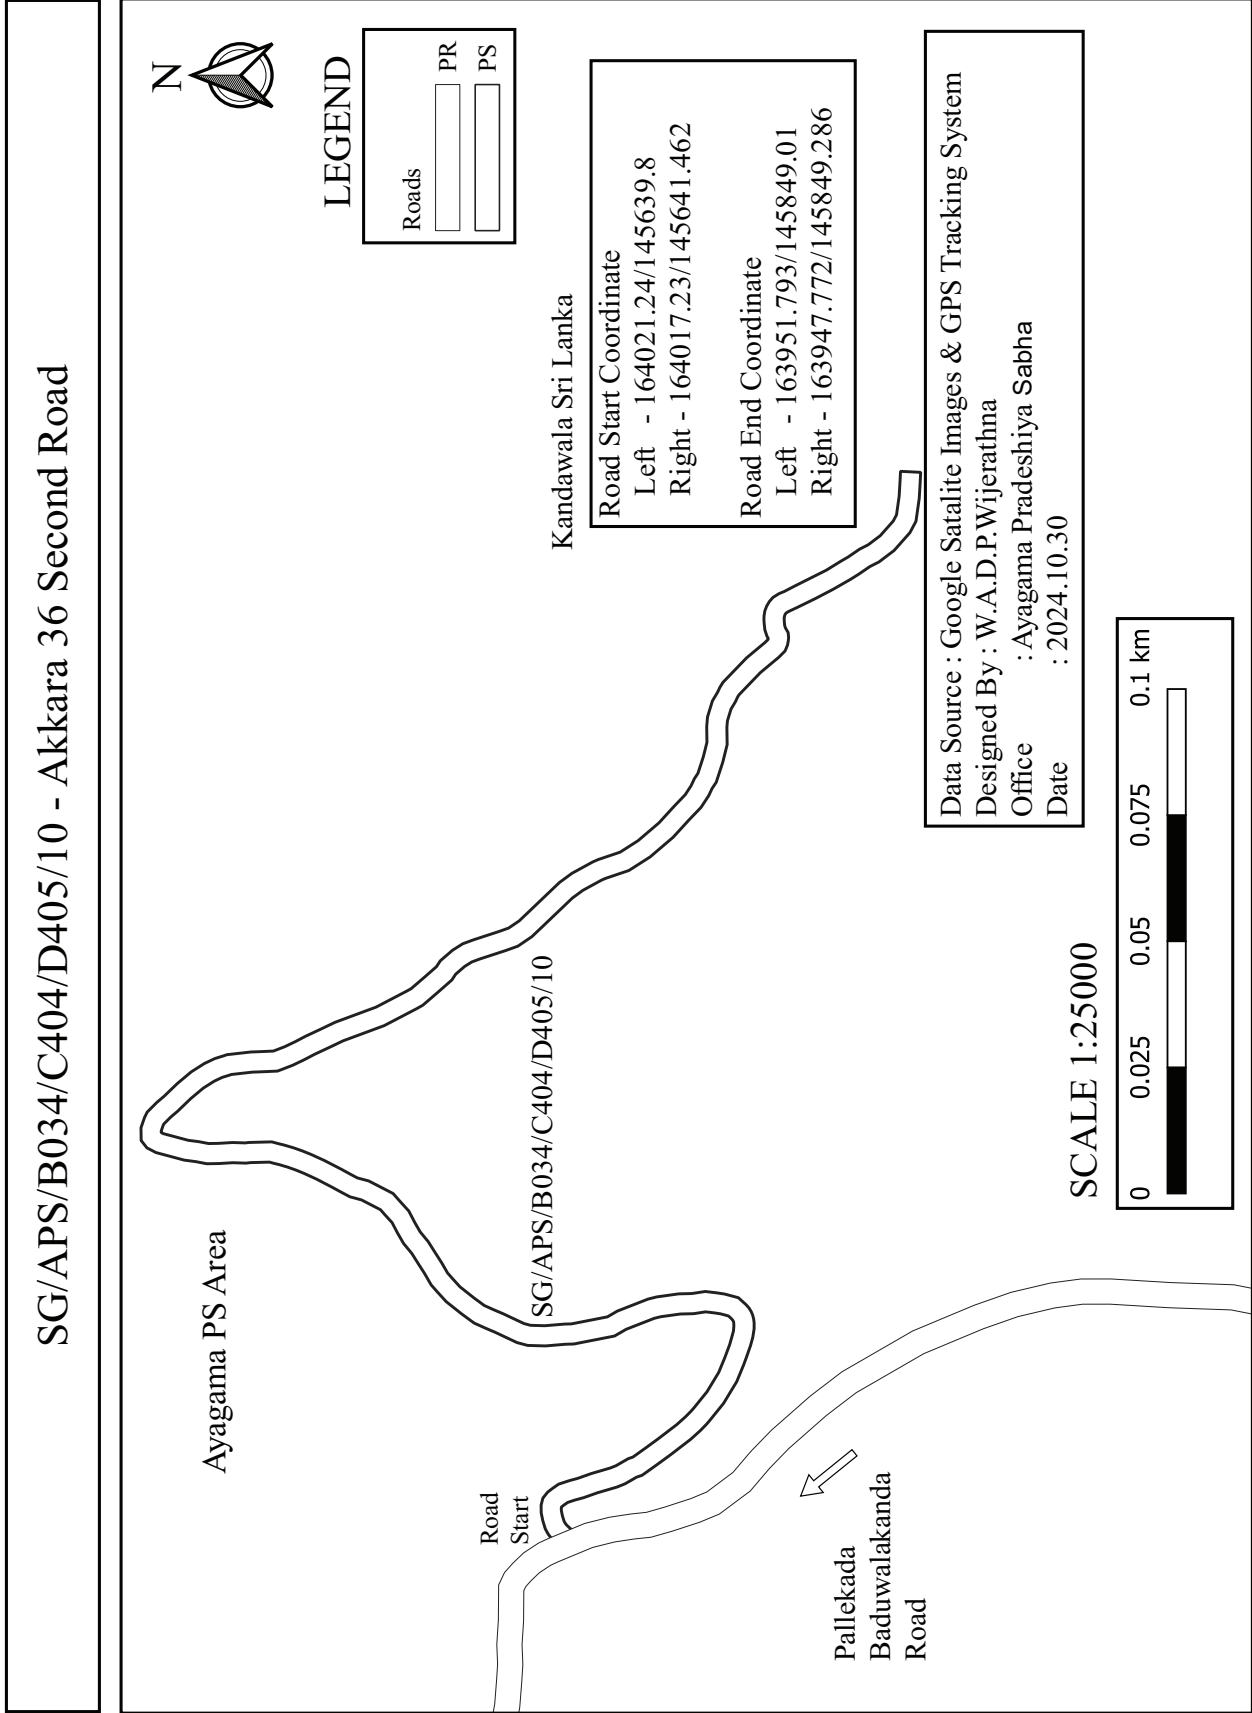


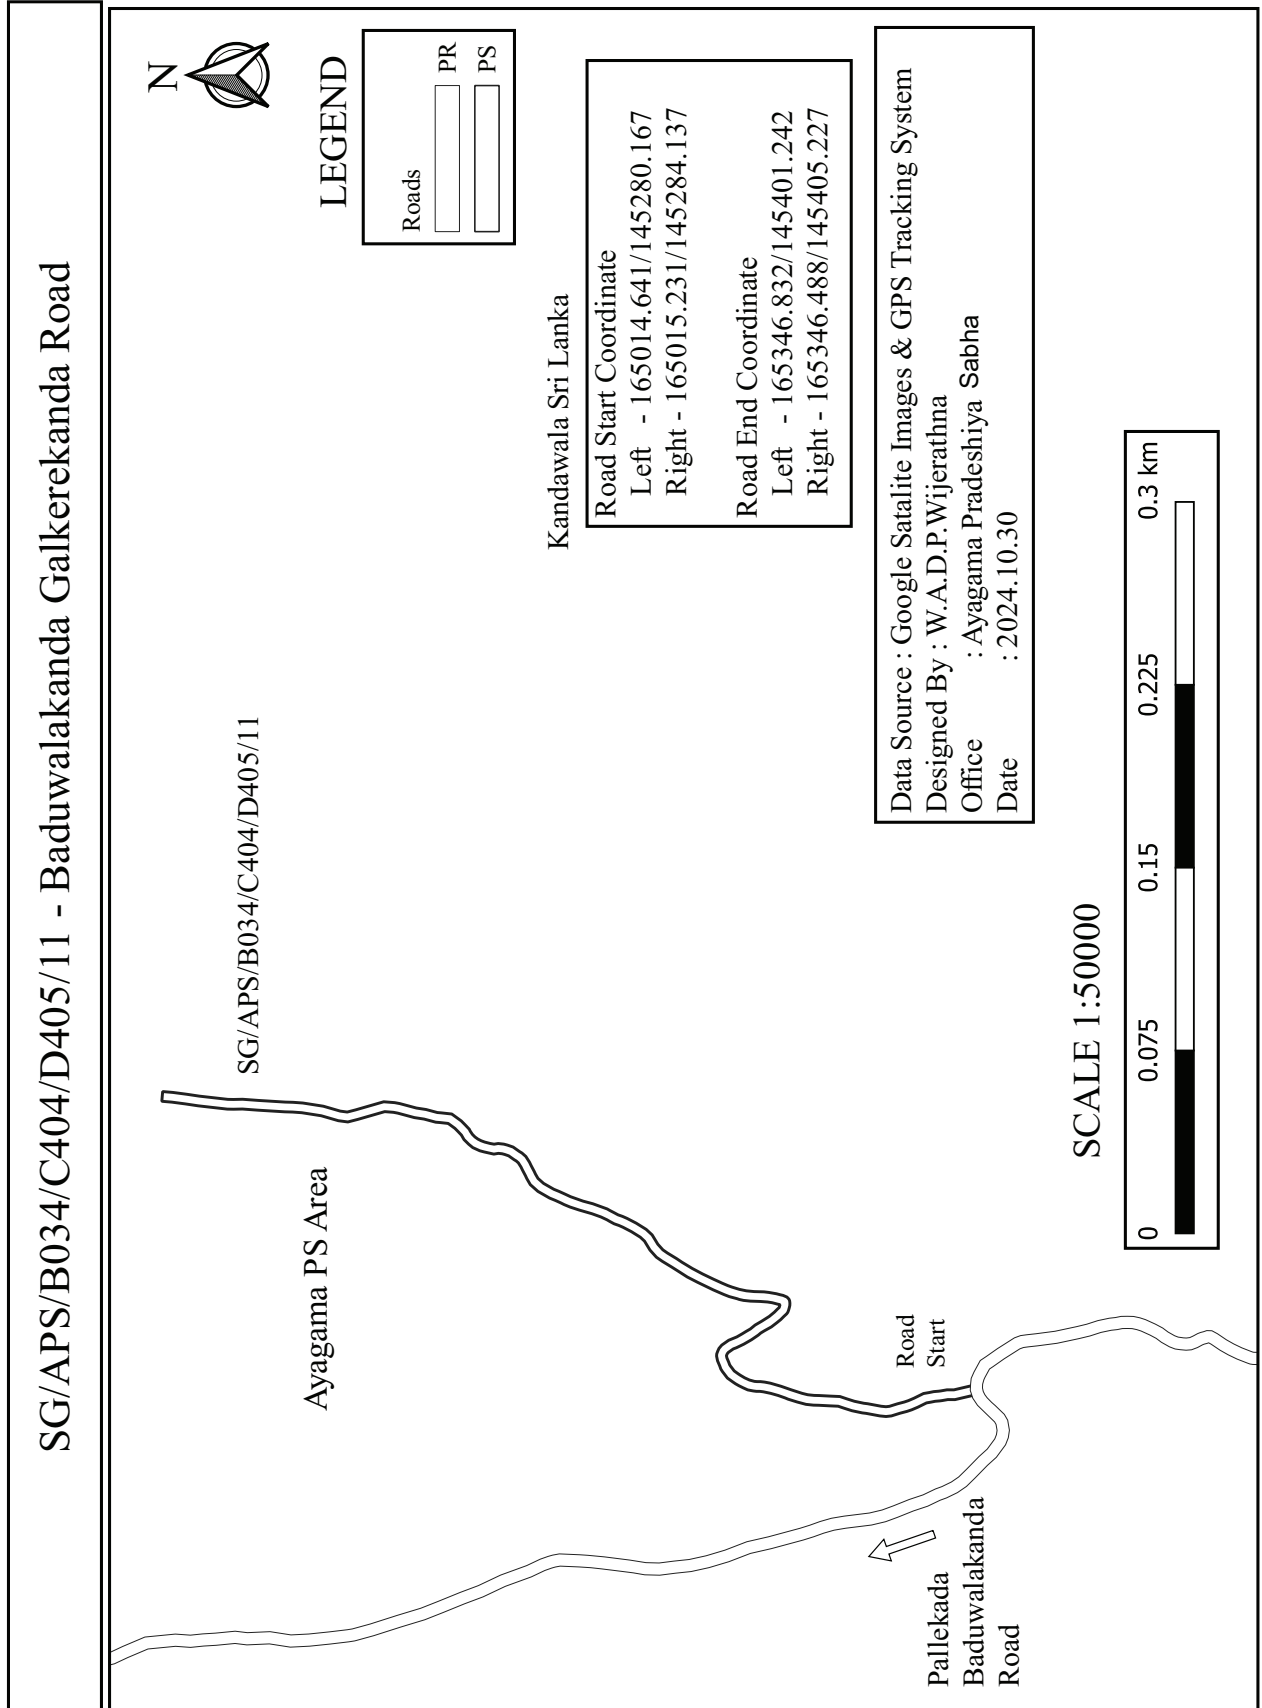


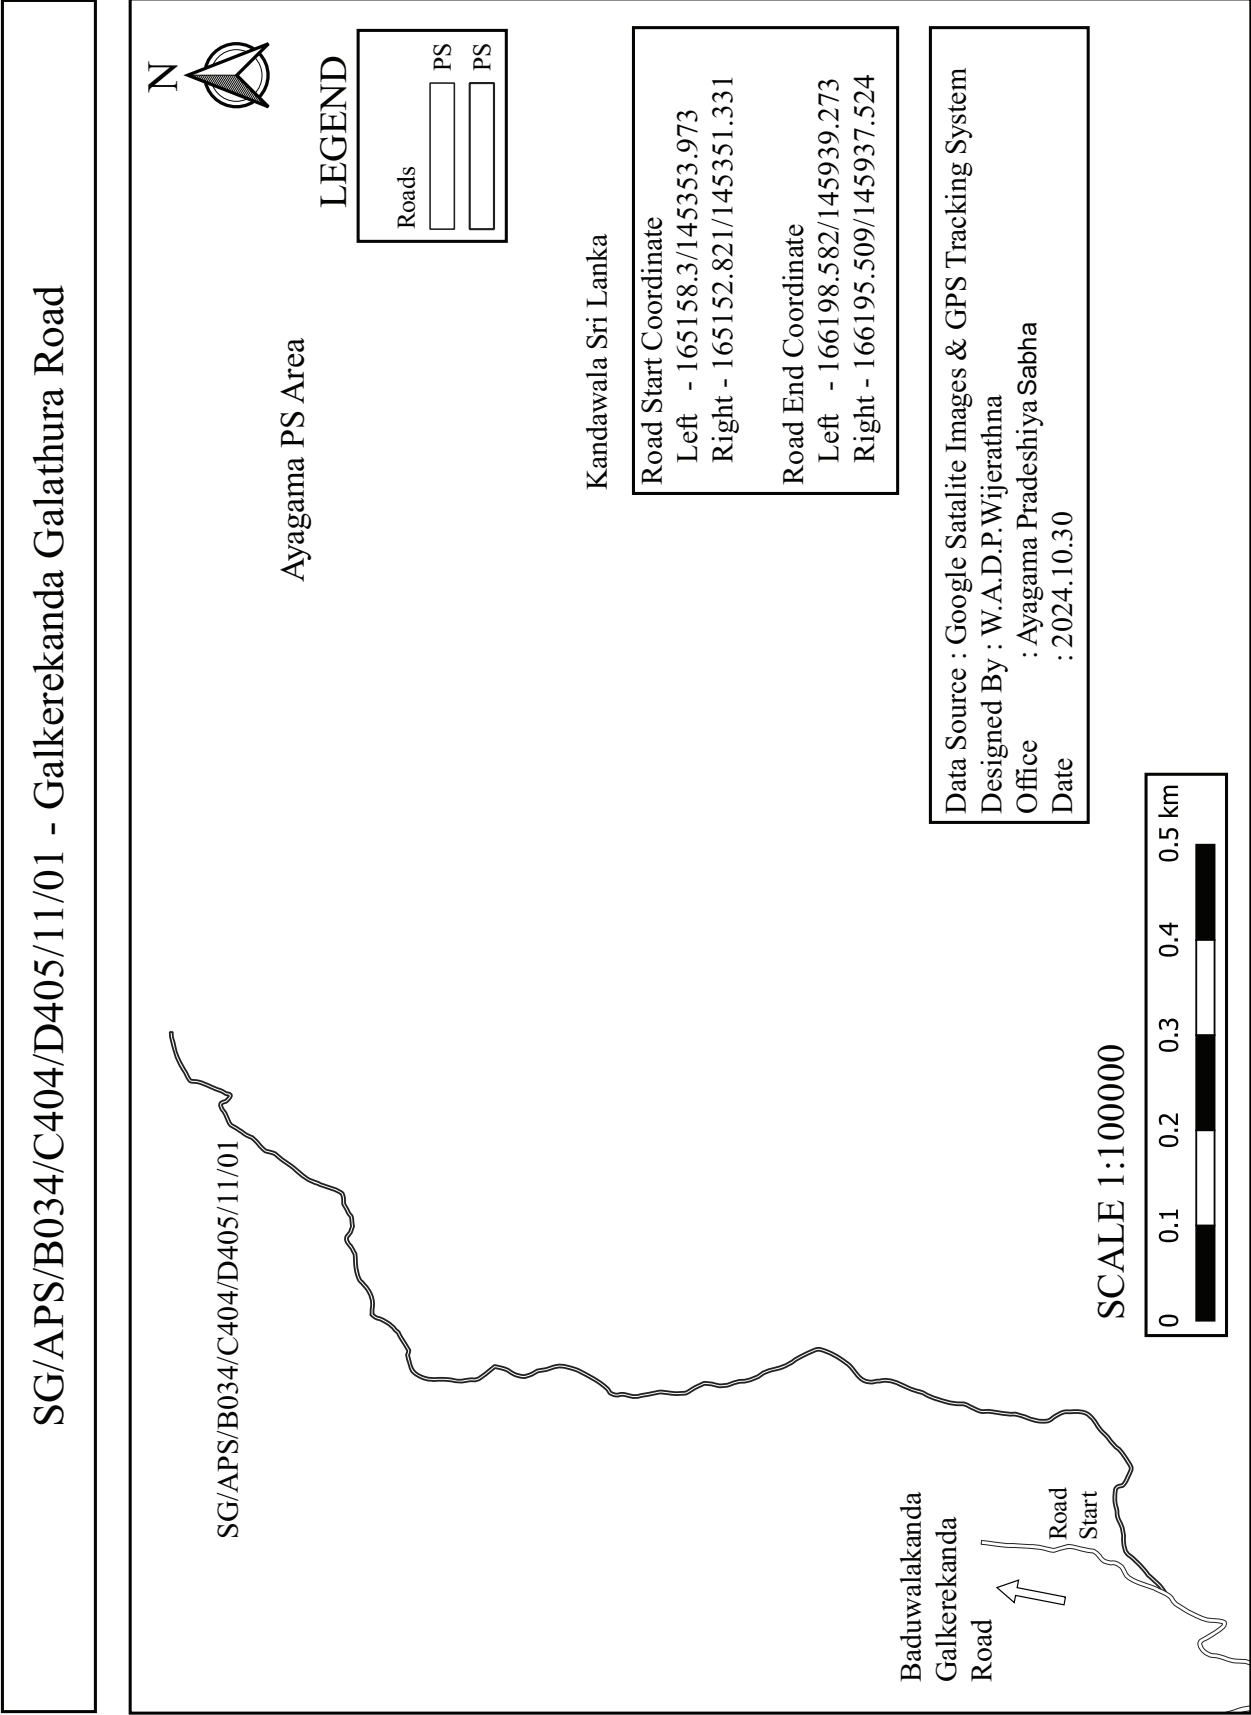


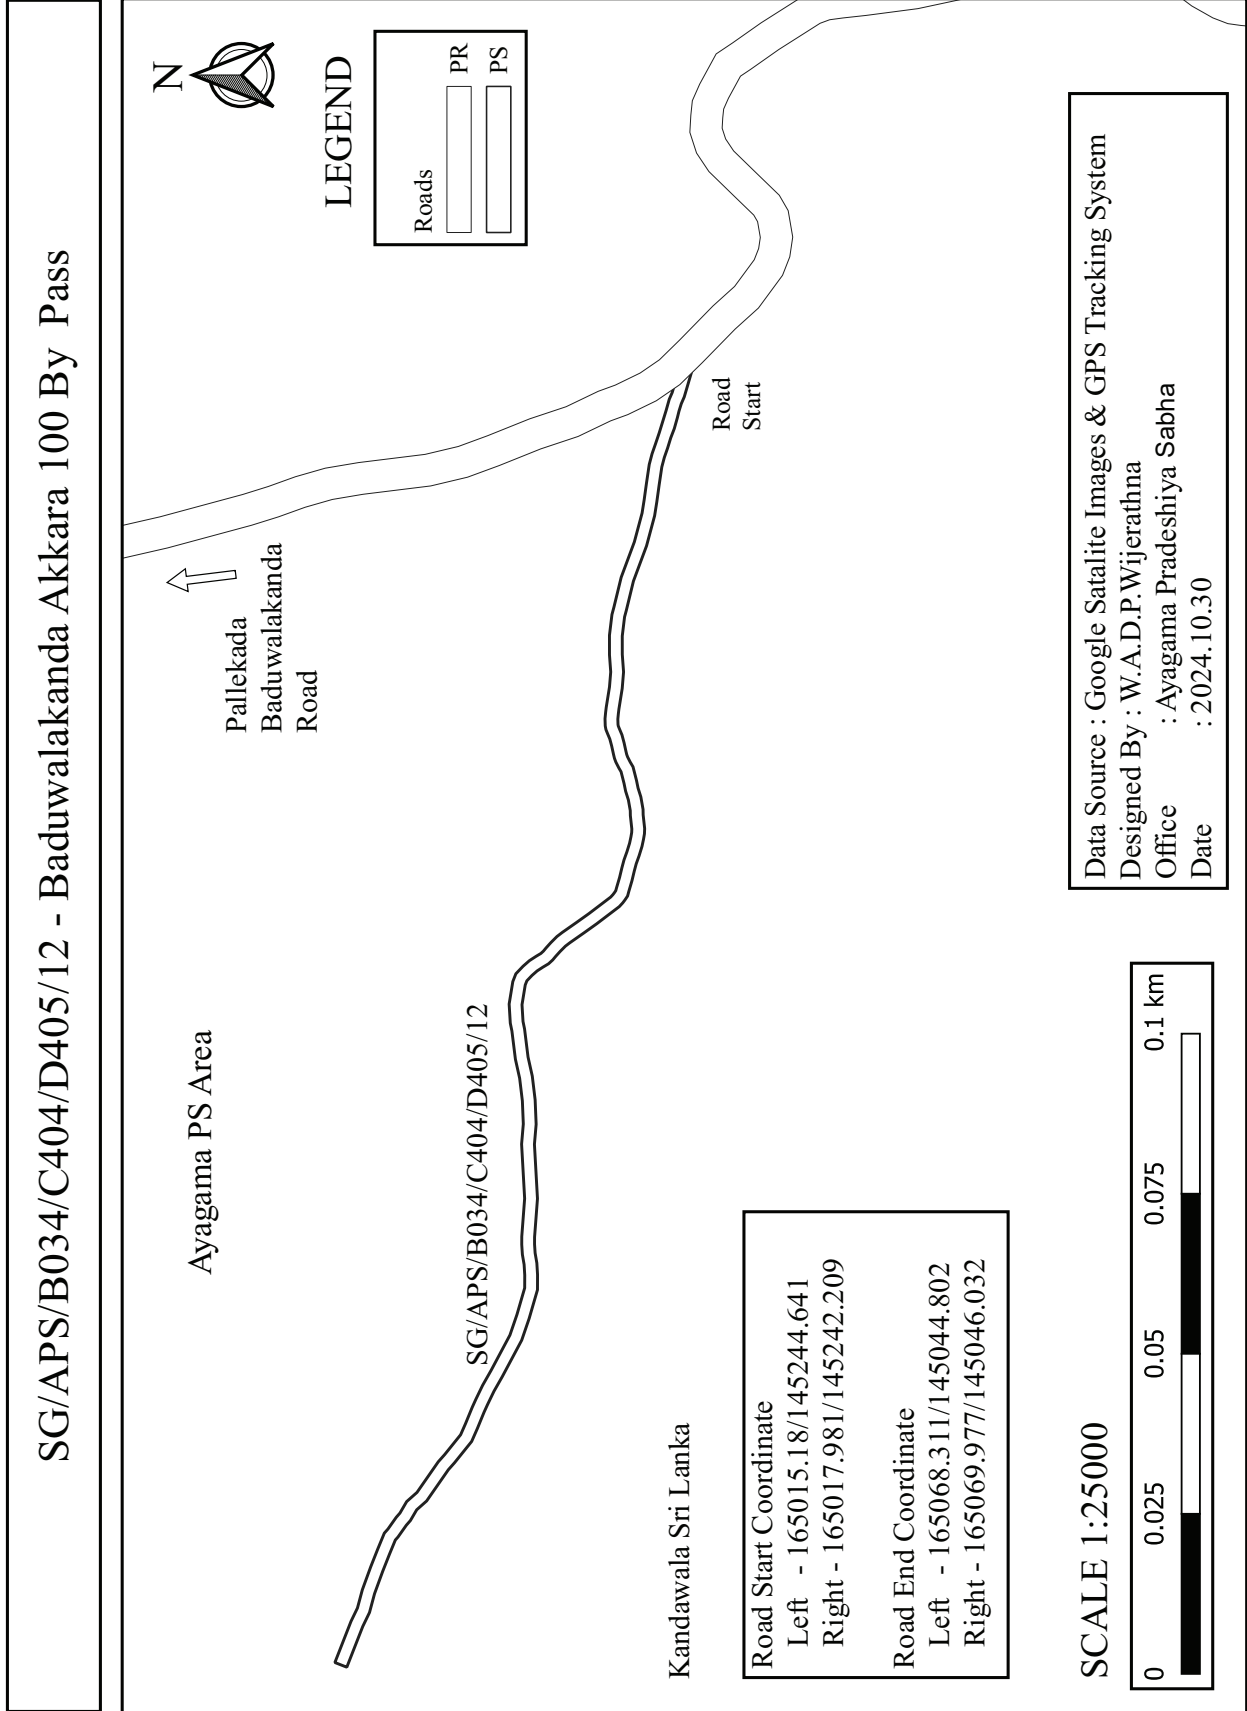

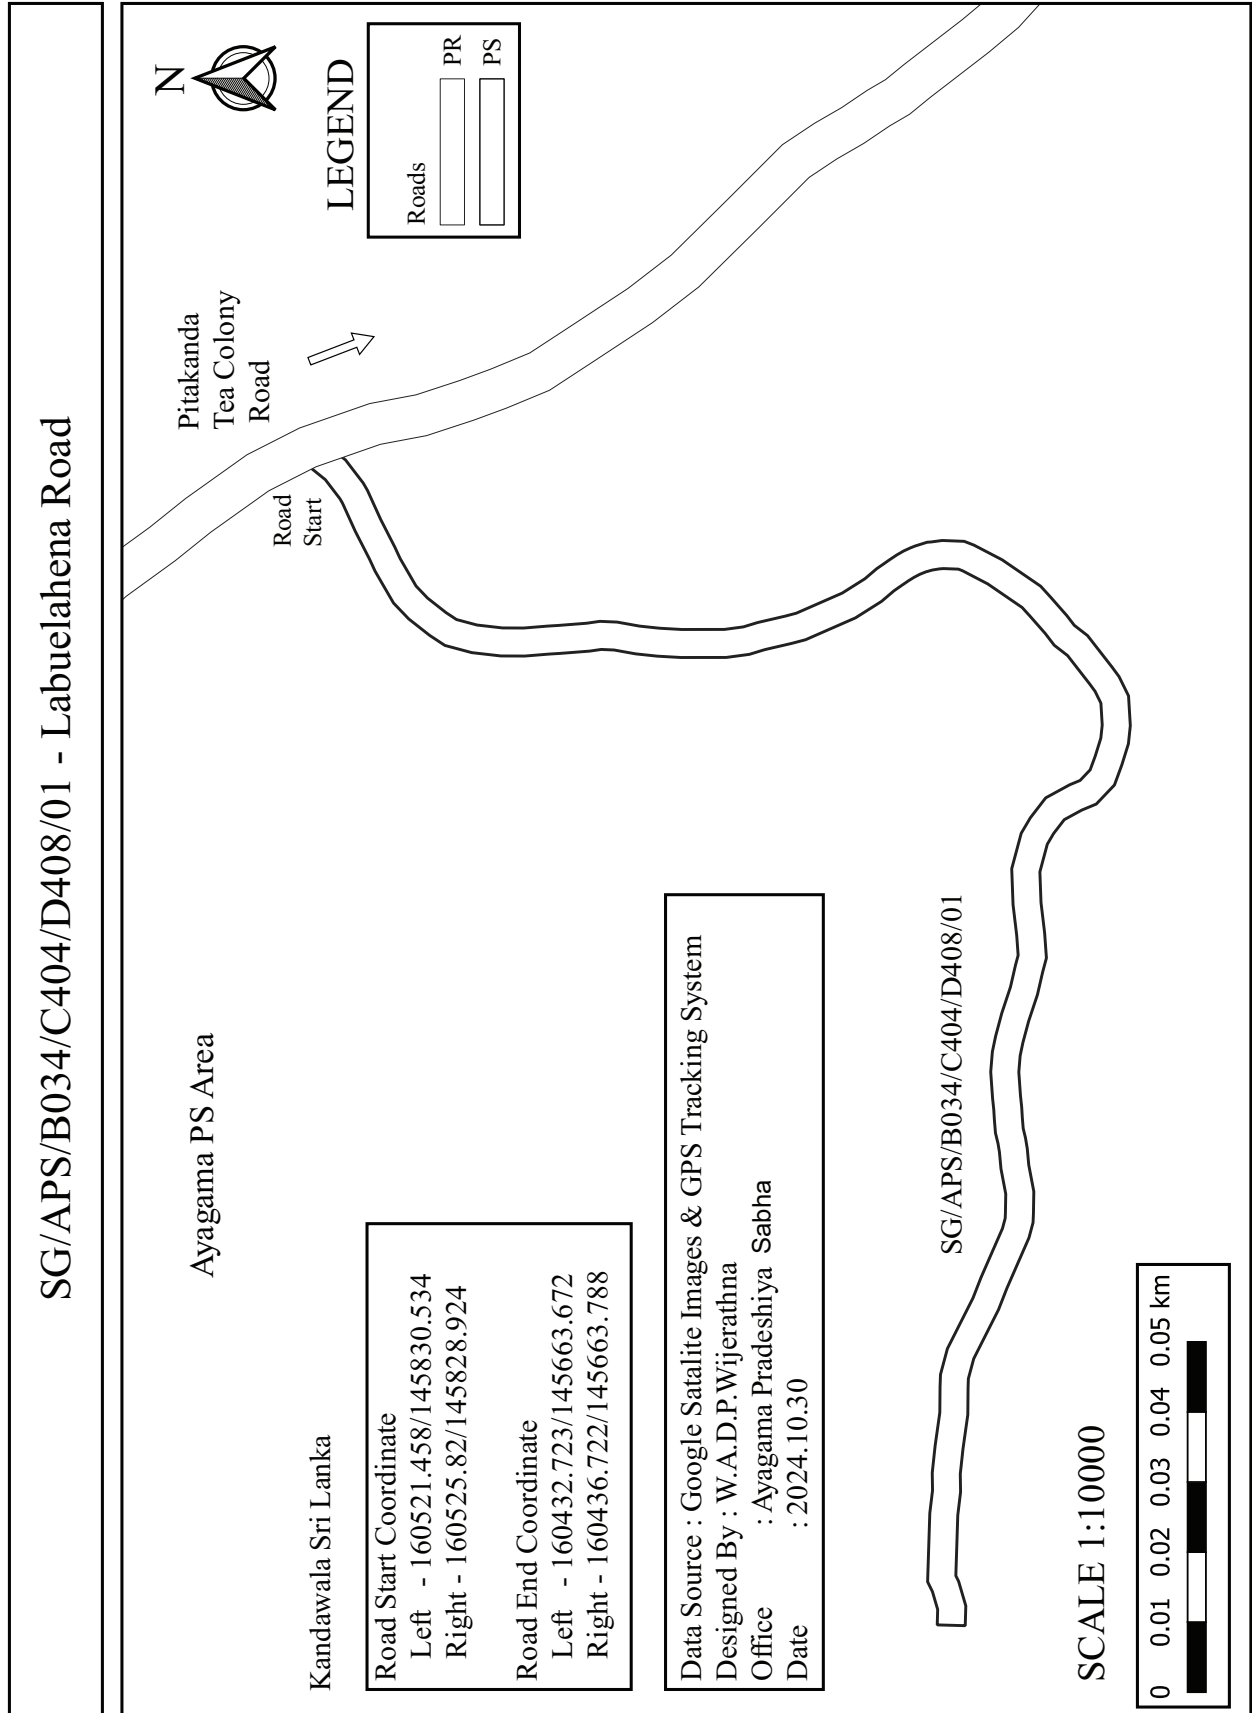


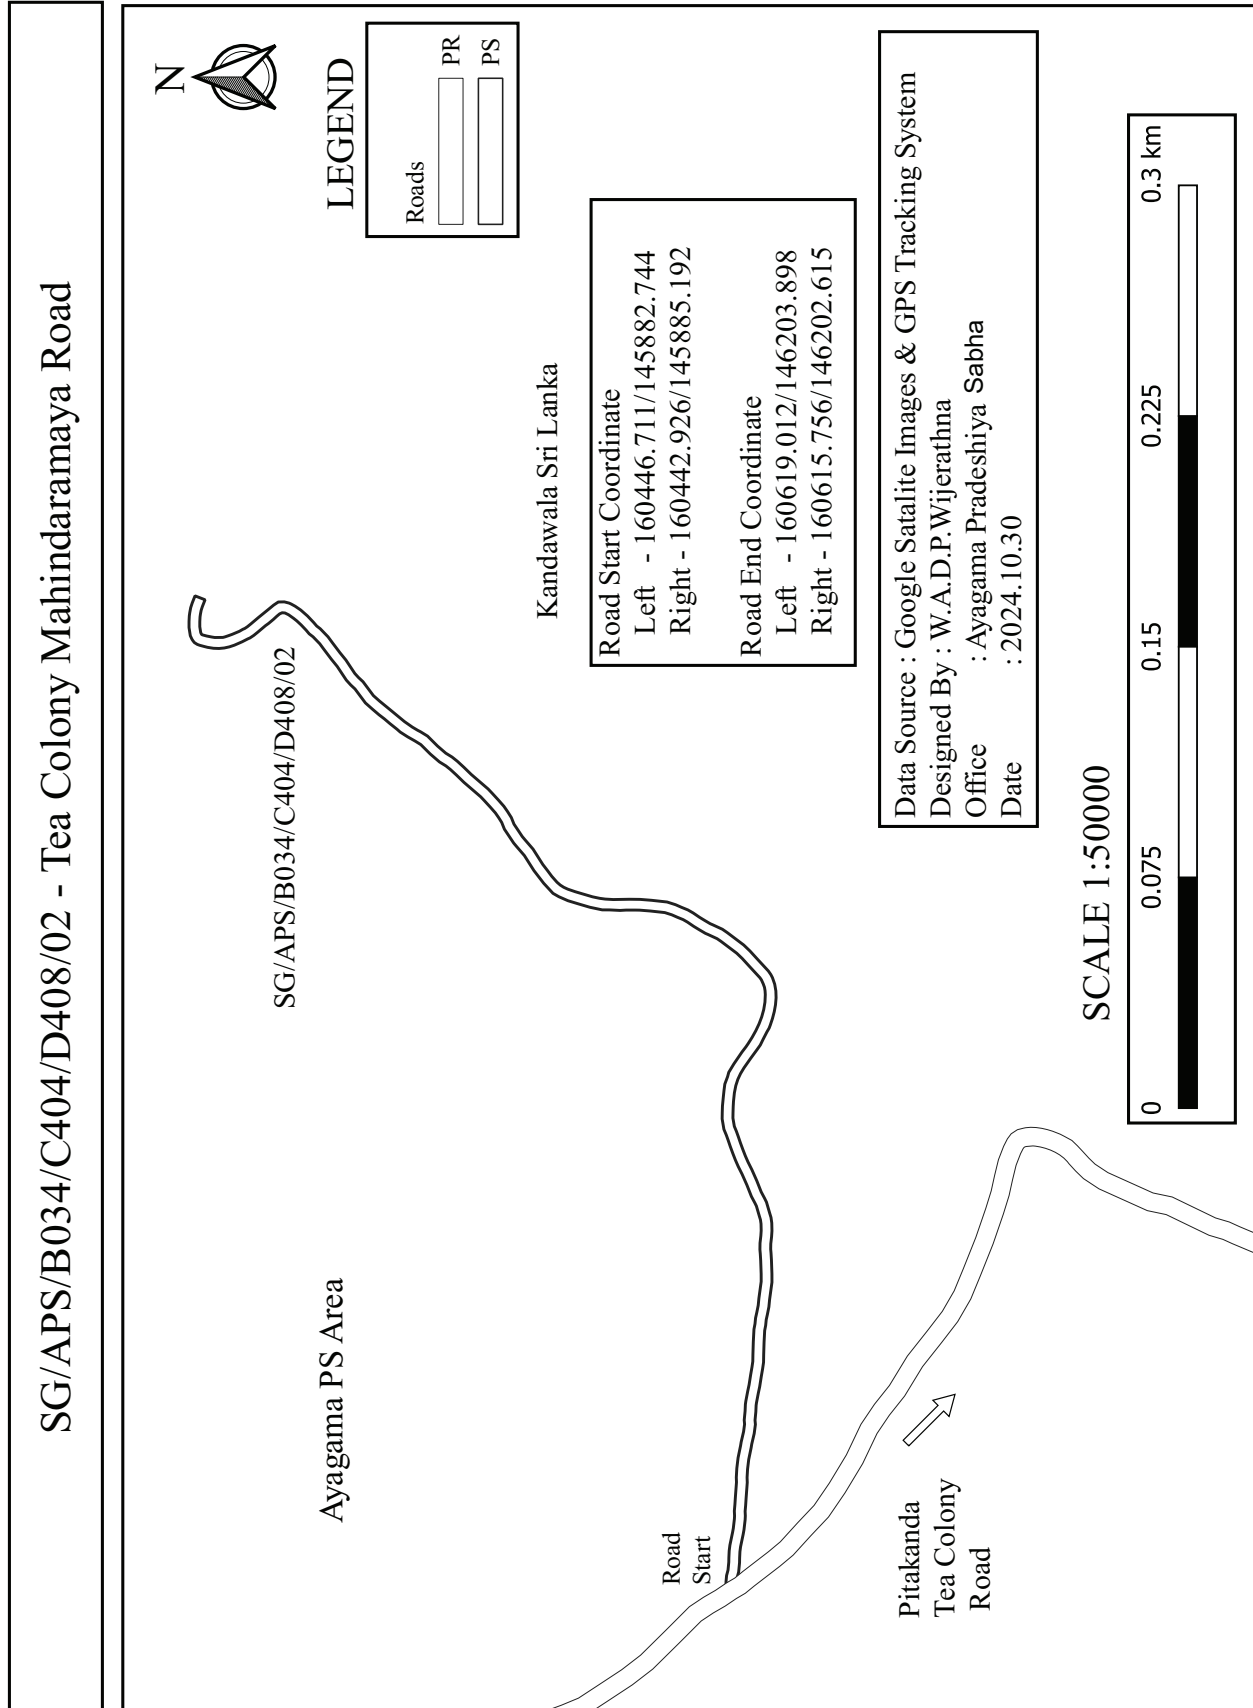


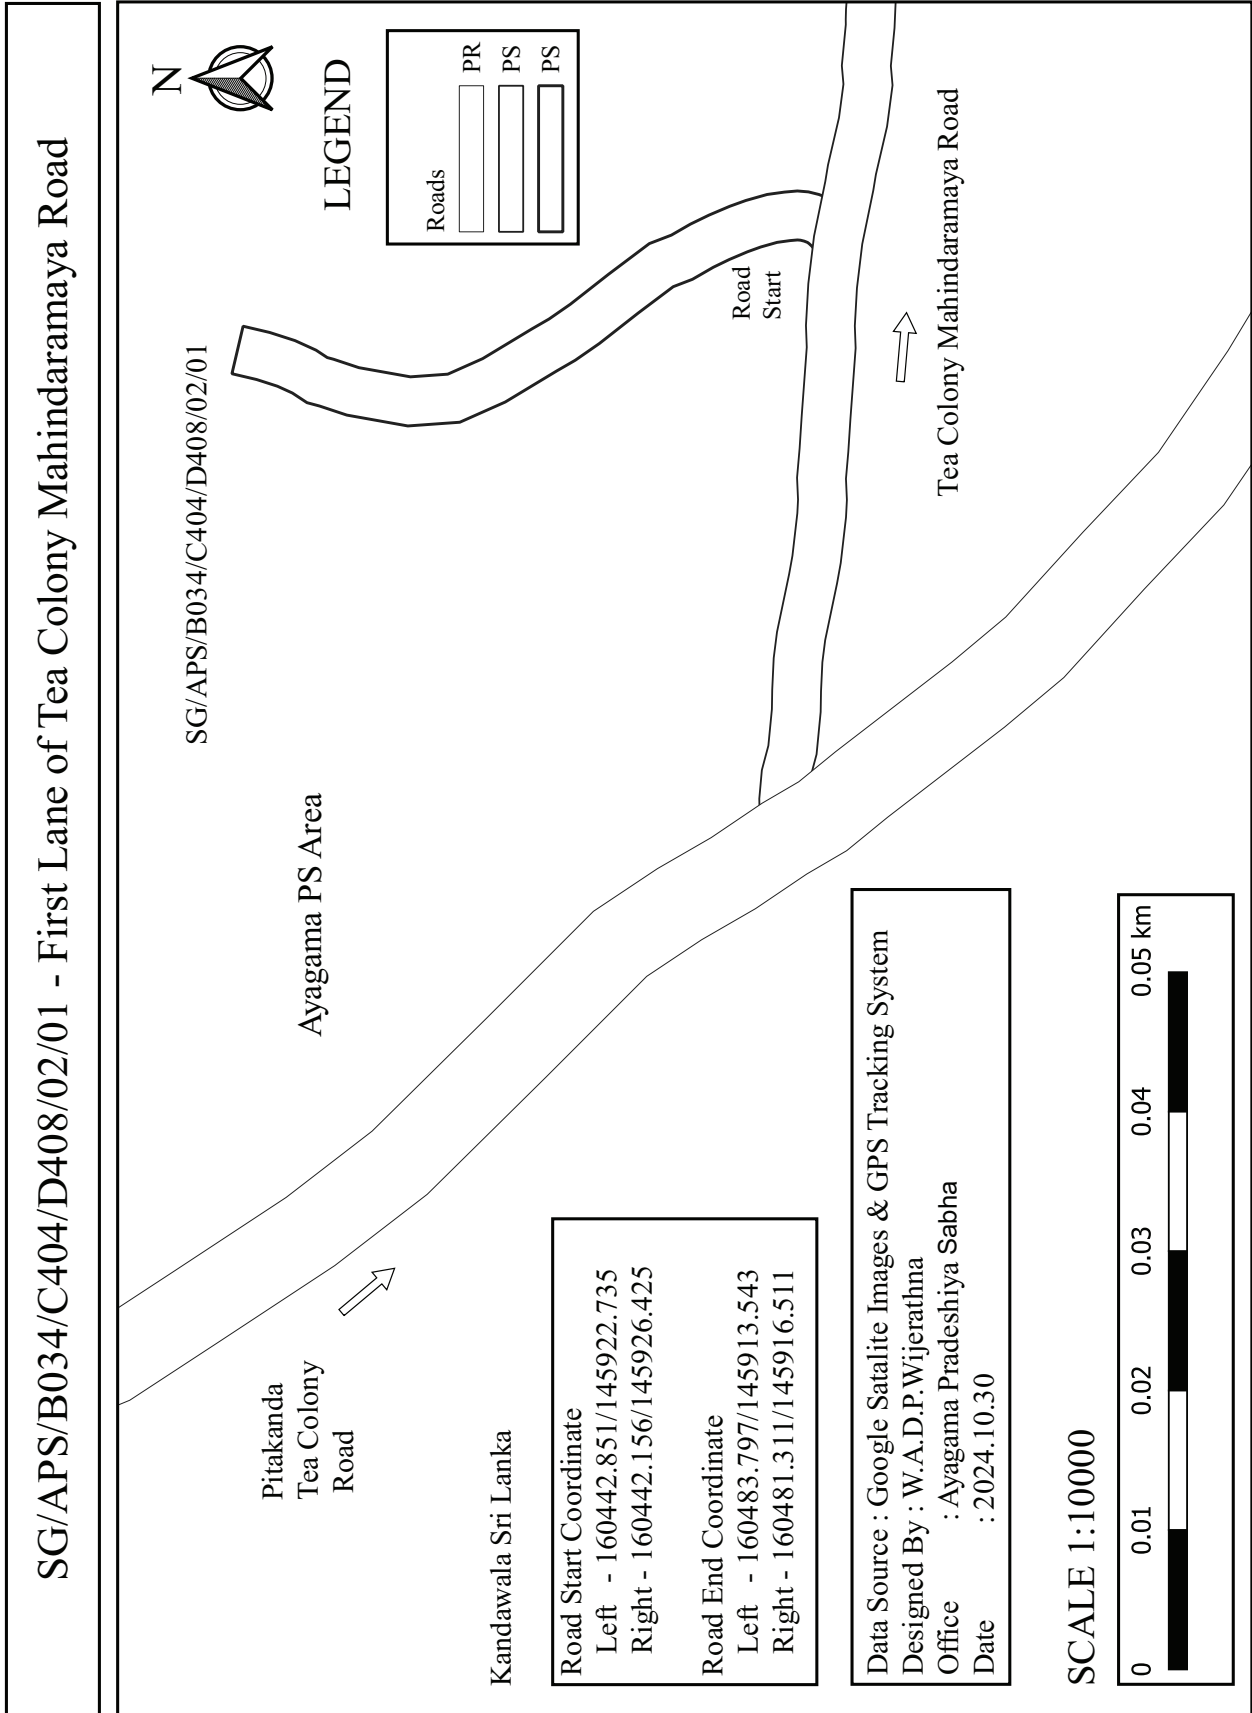


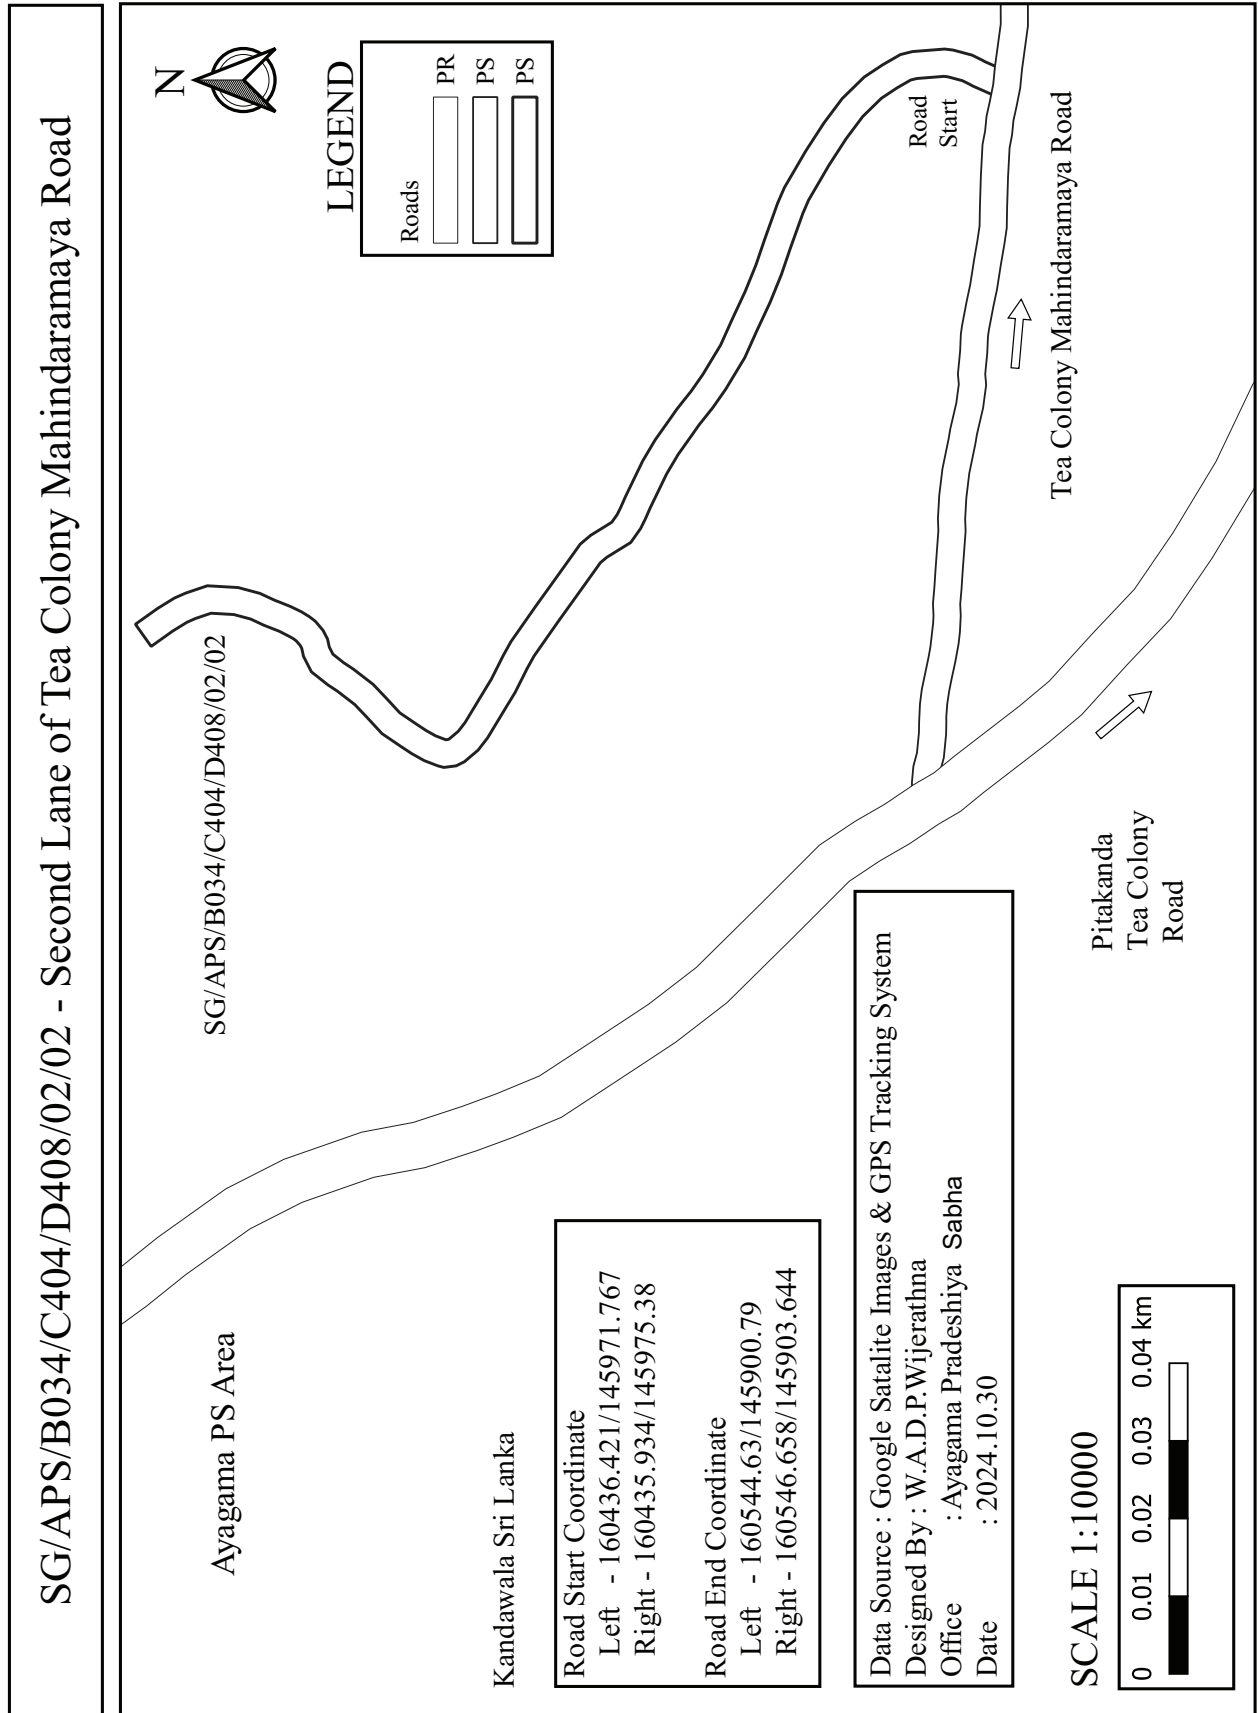



SG/APS/B034/C404/D408/02/02/01 - First By Pass of Second Lane of Tea Colony
Mahindaramaya Road

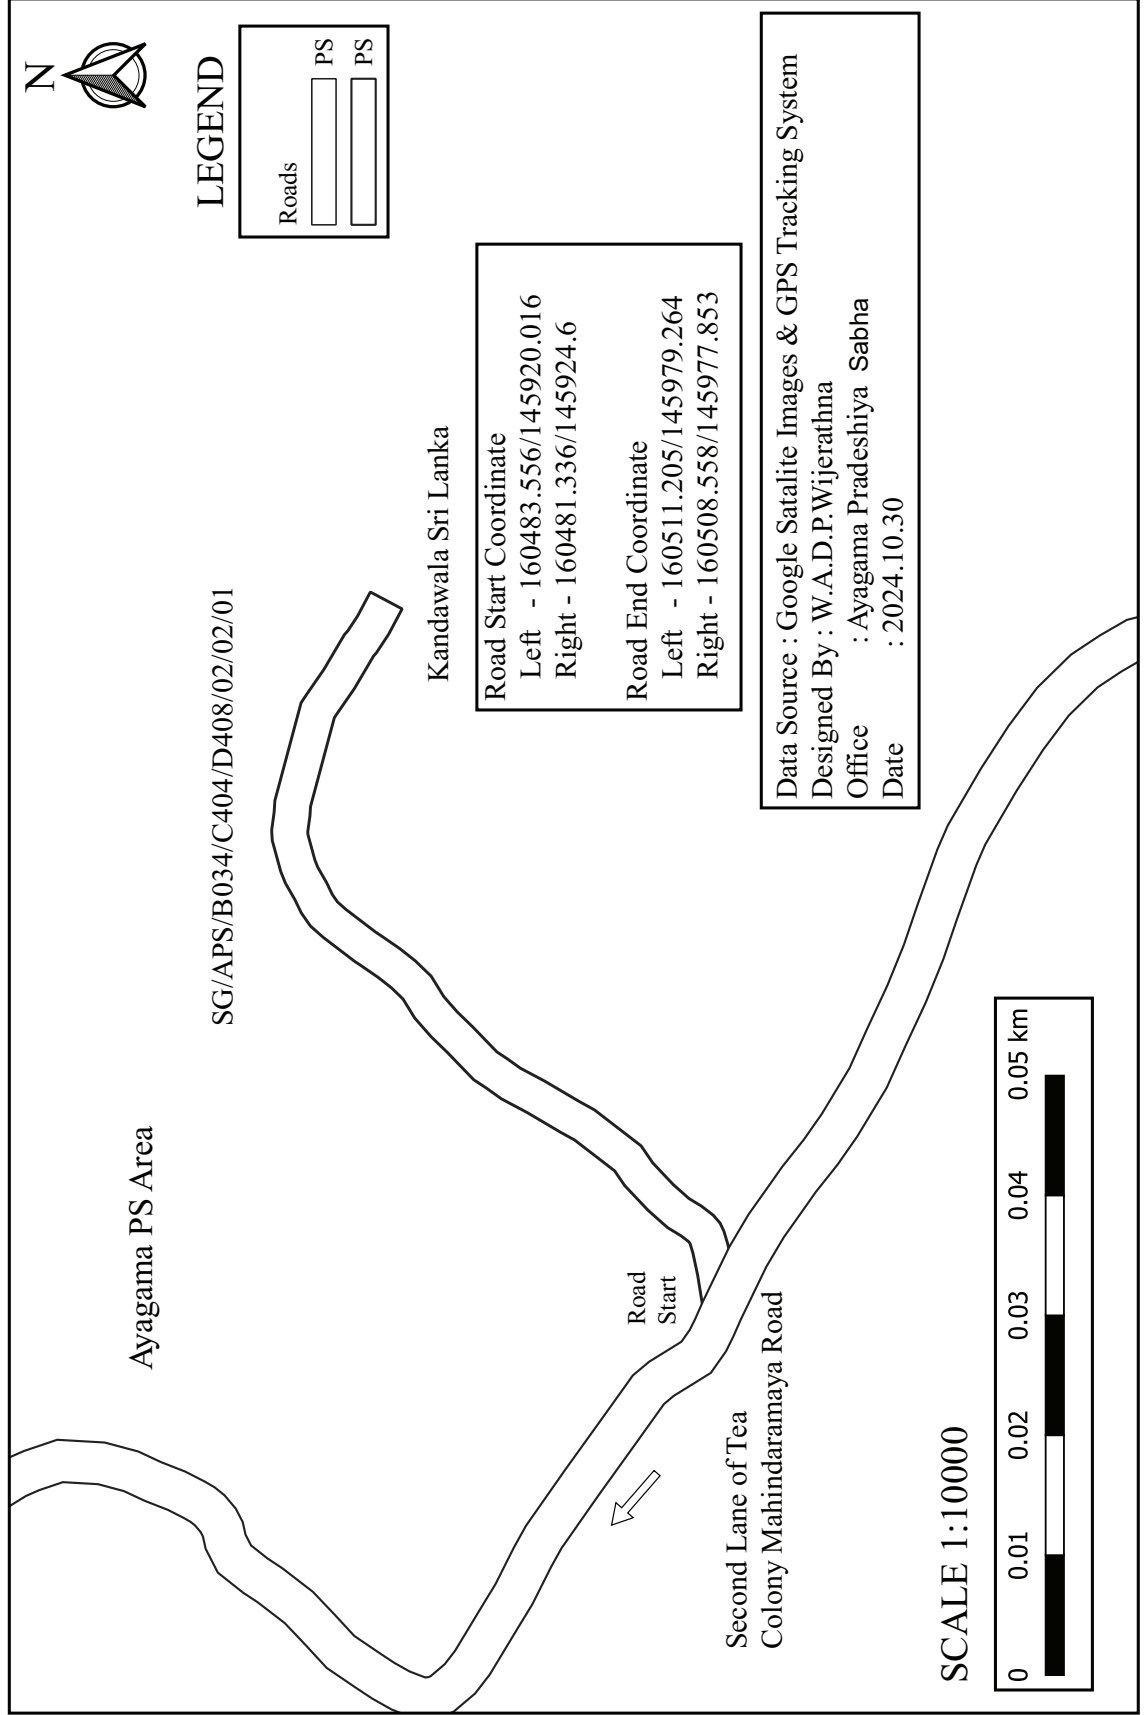


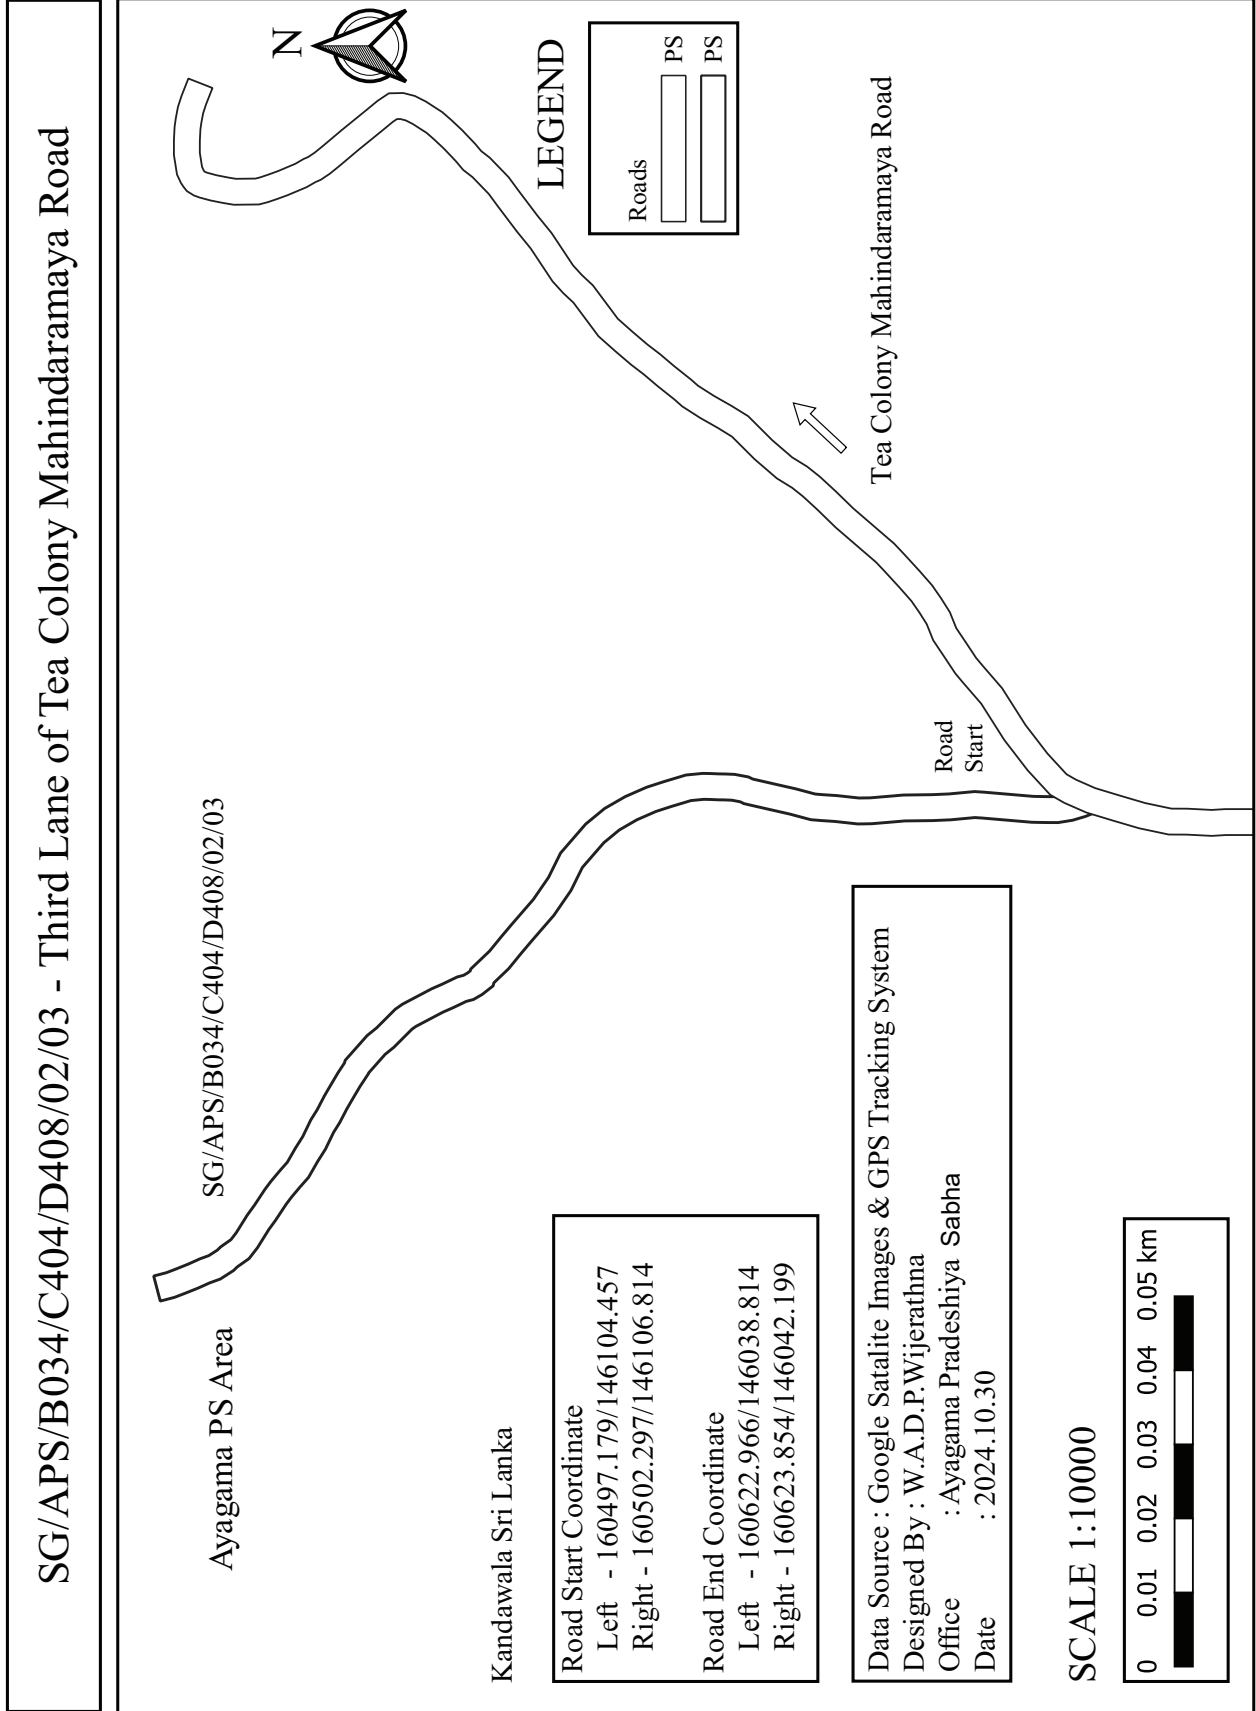


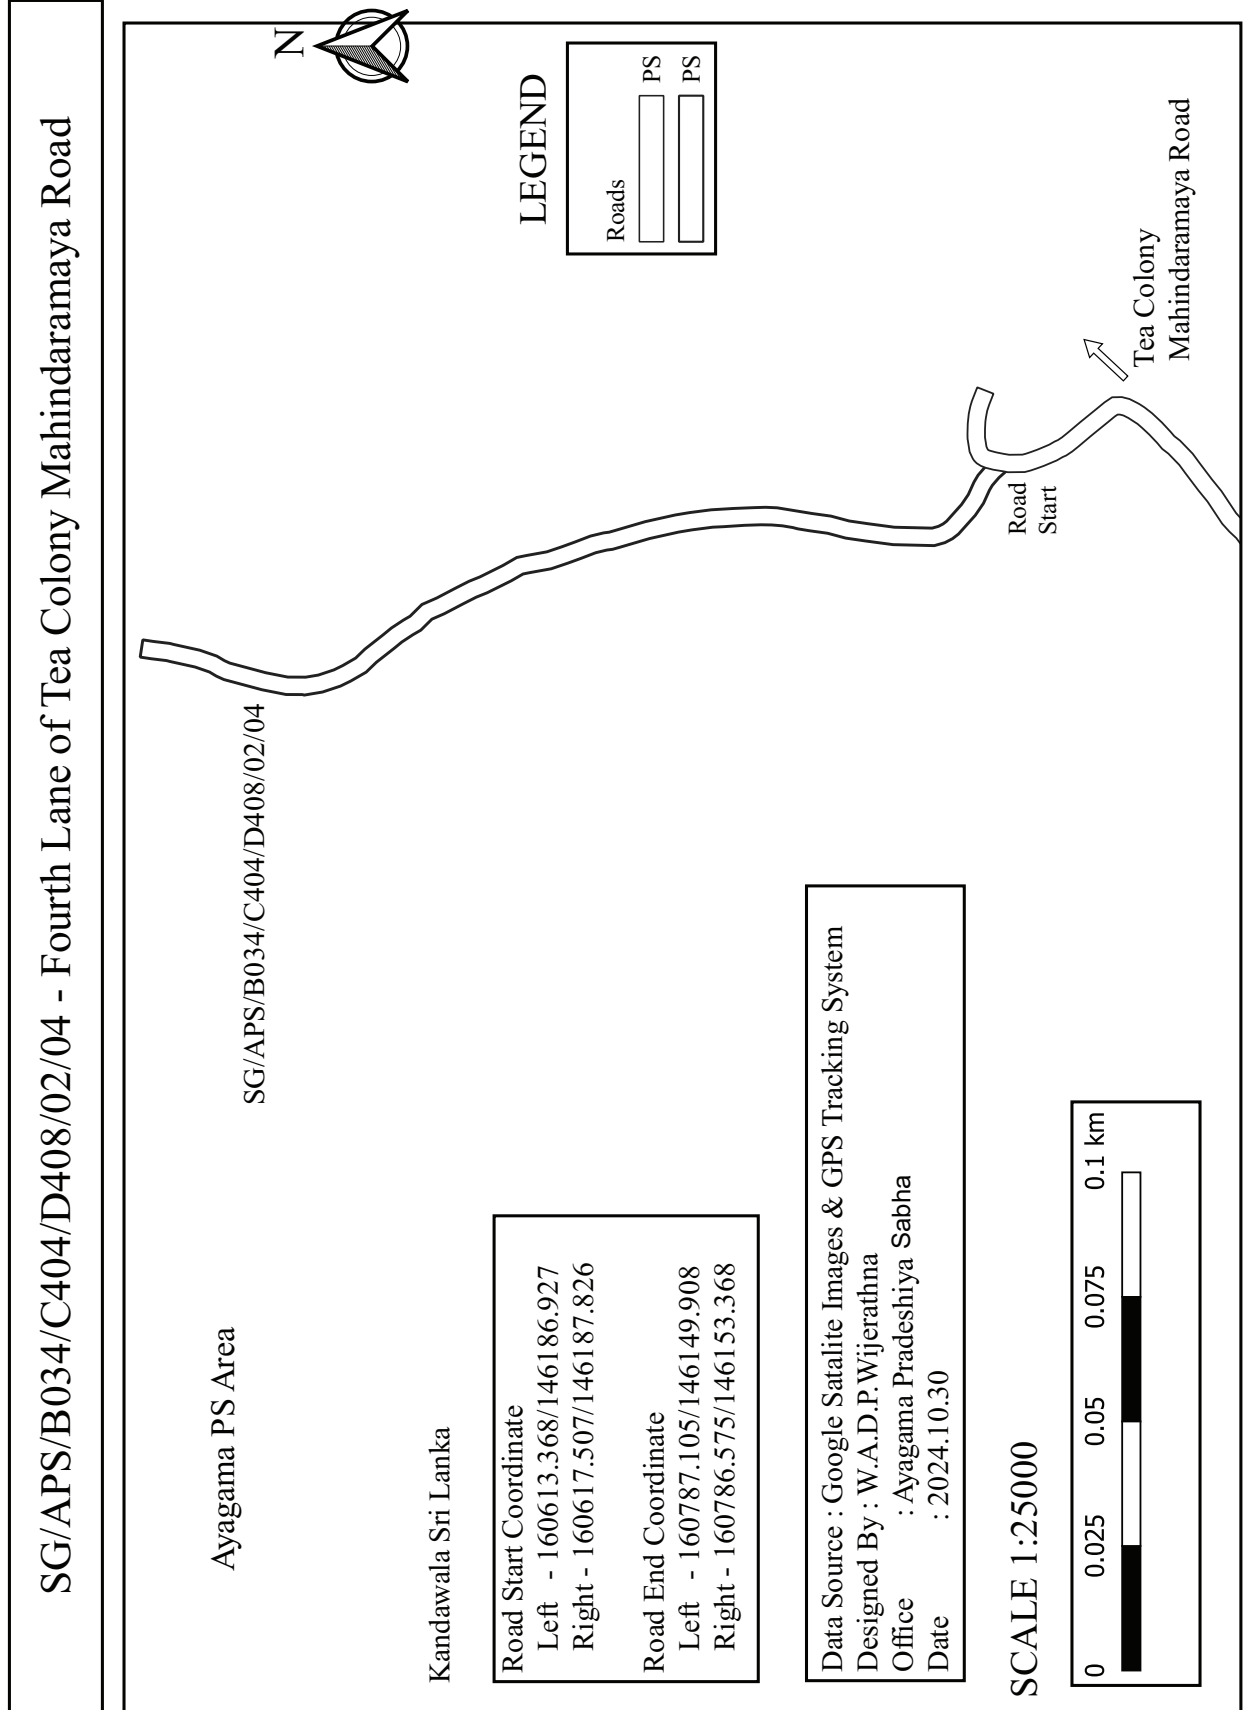

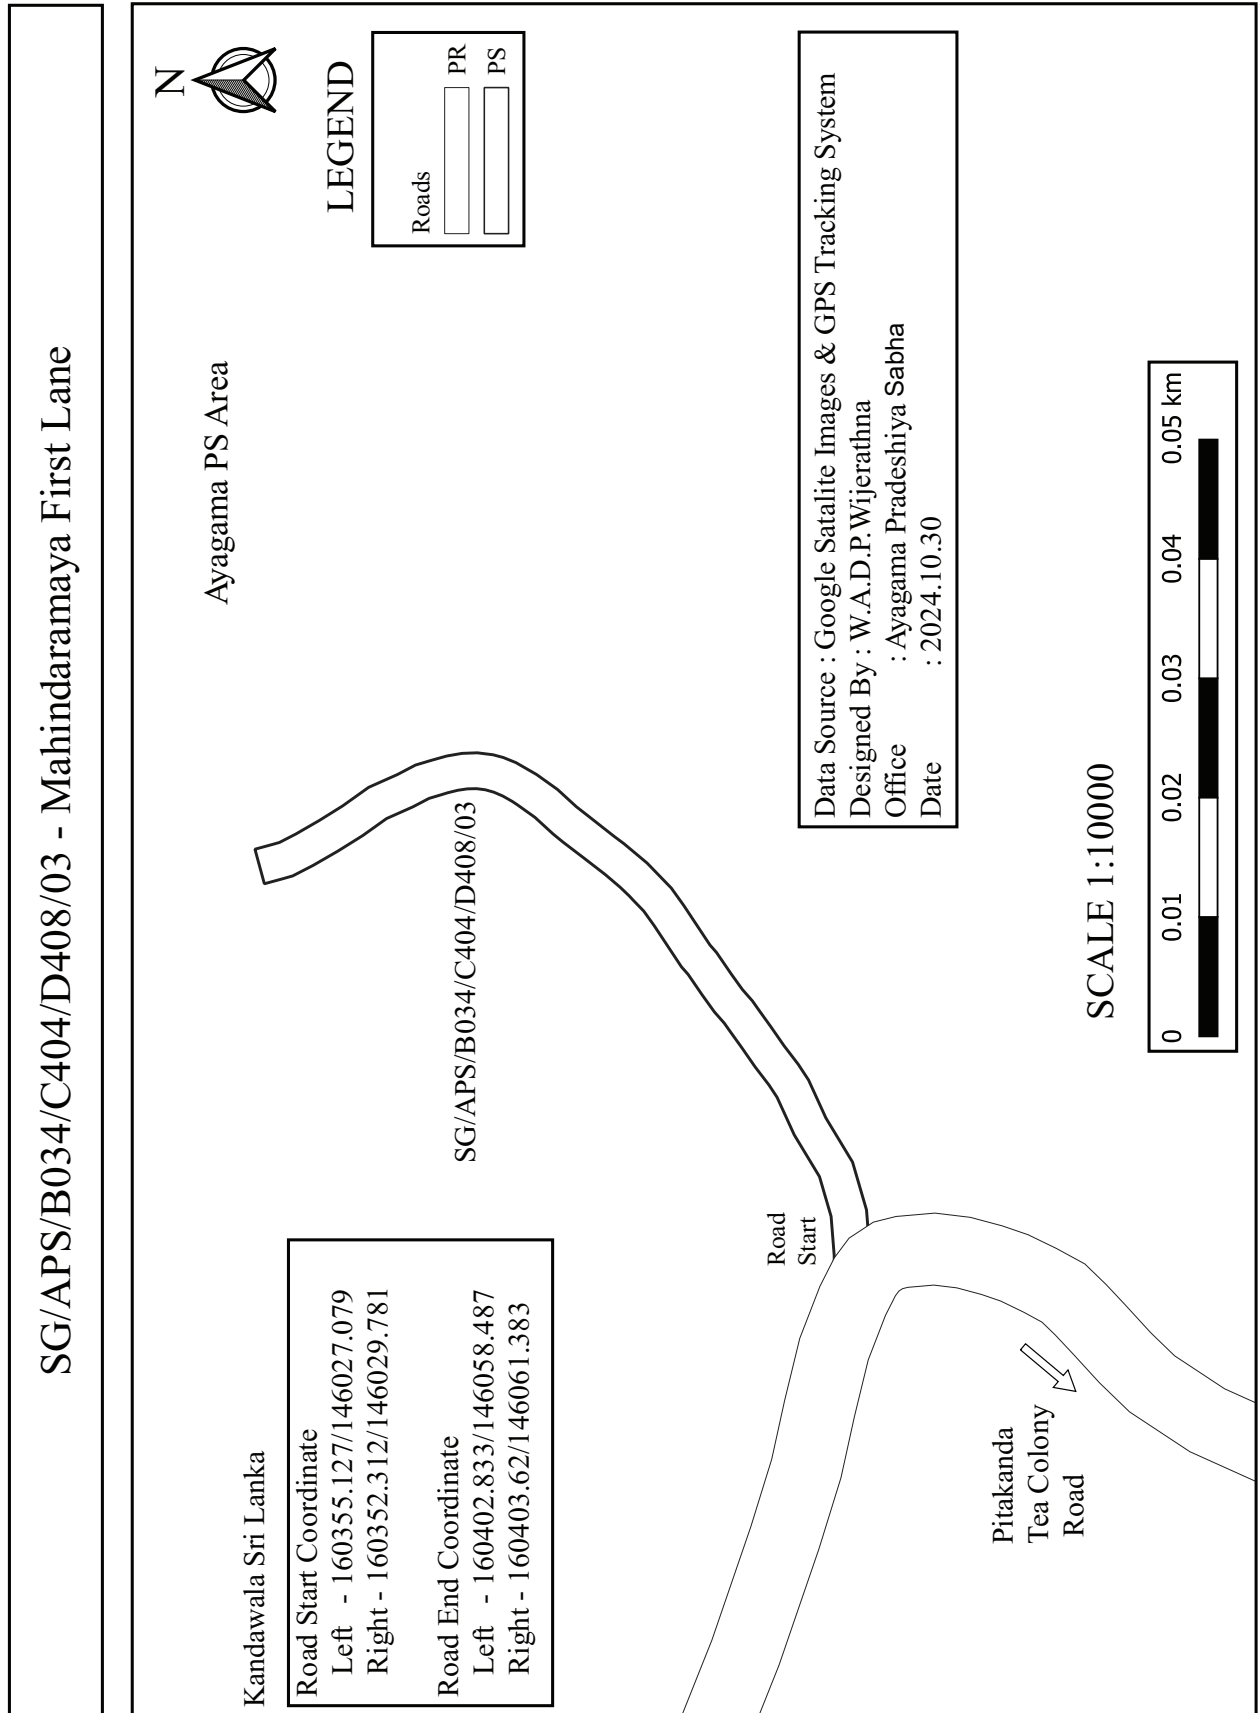


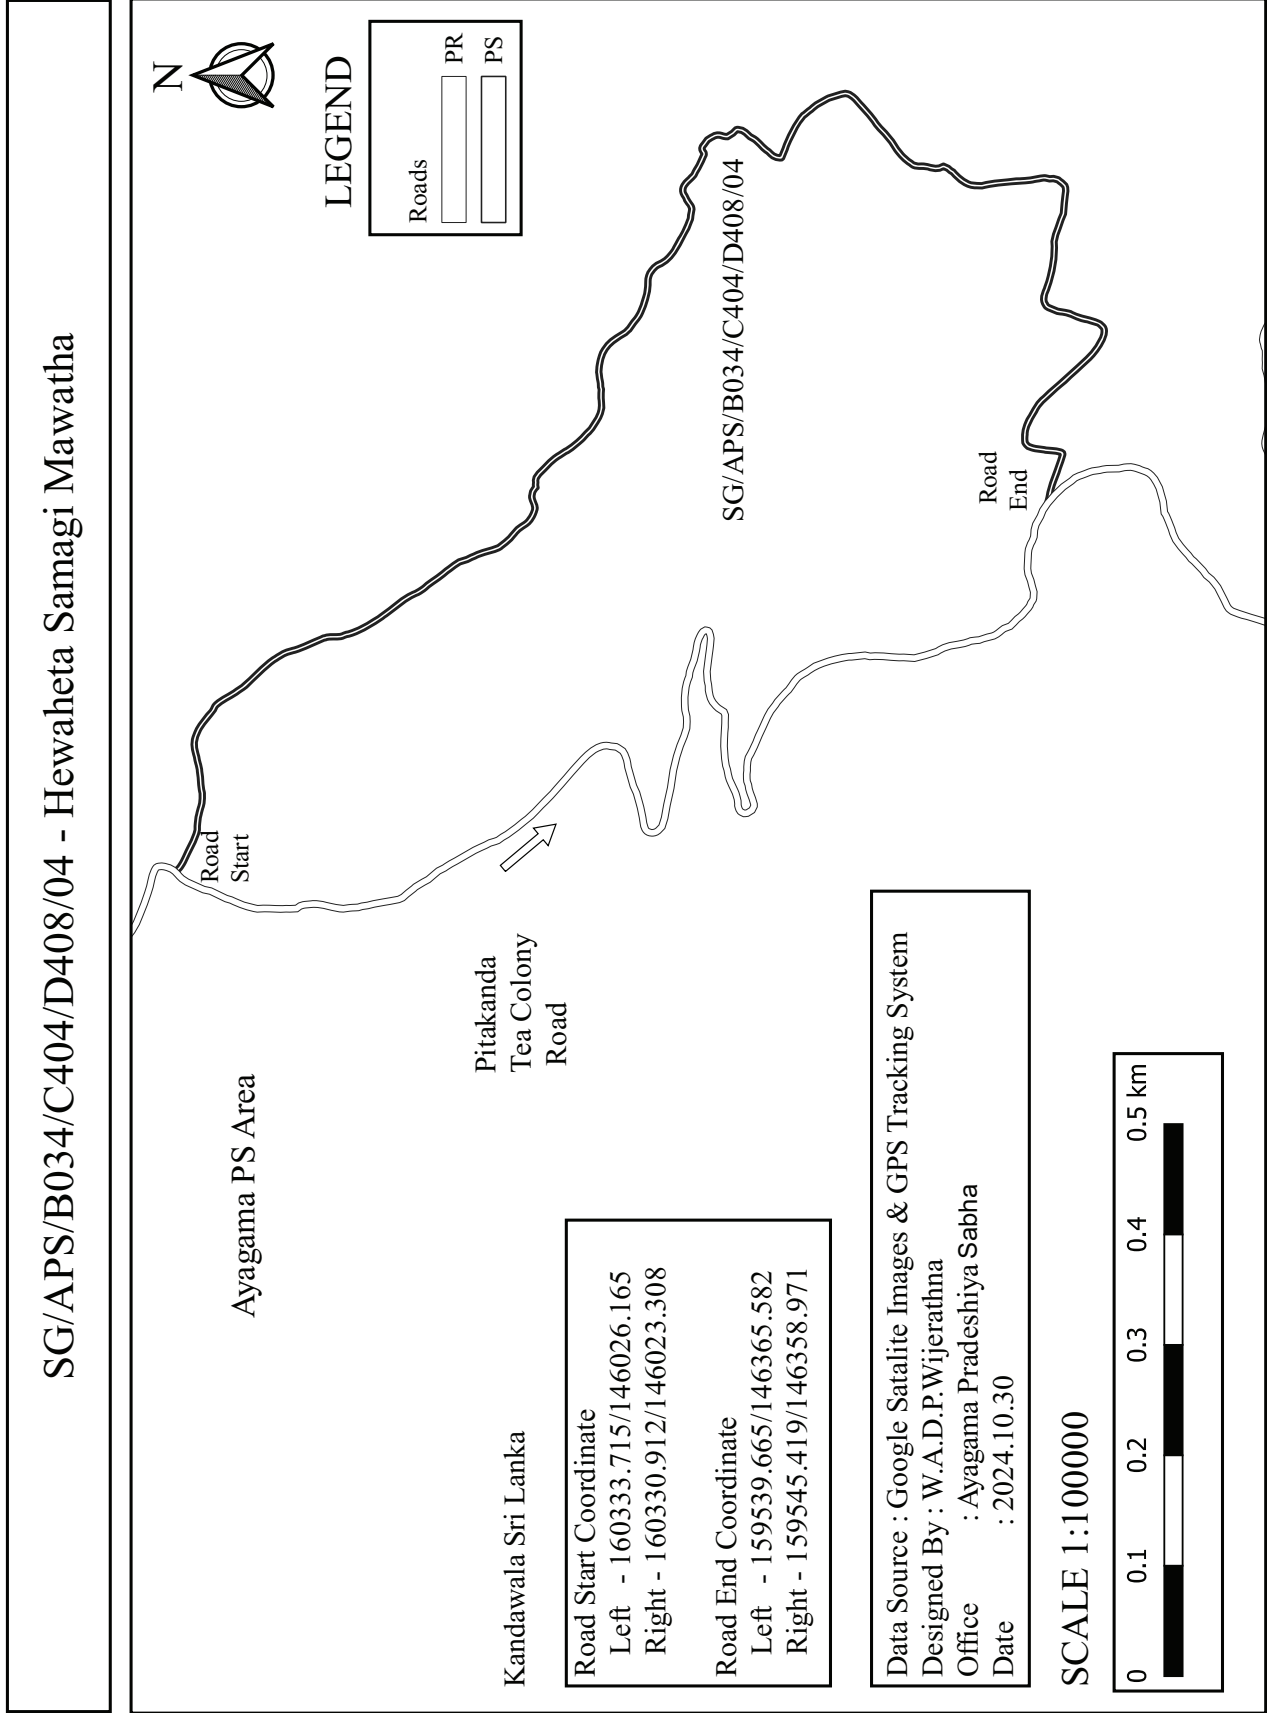


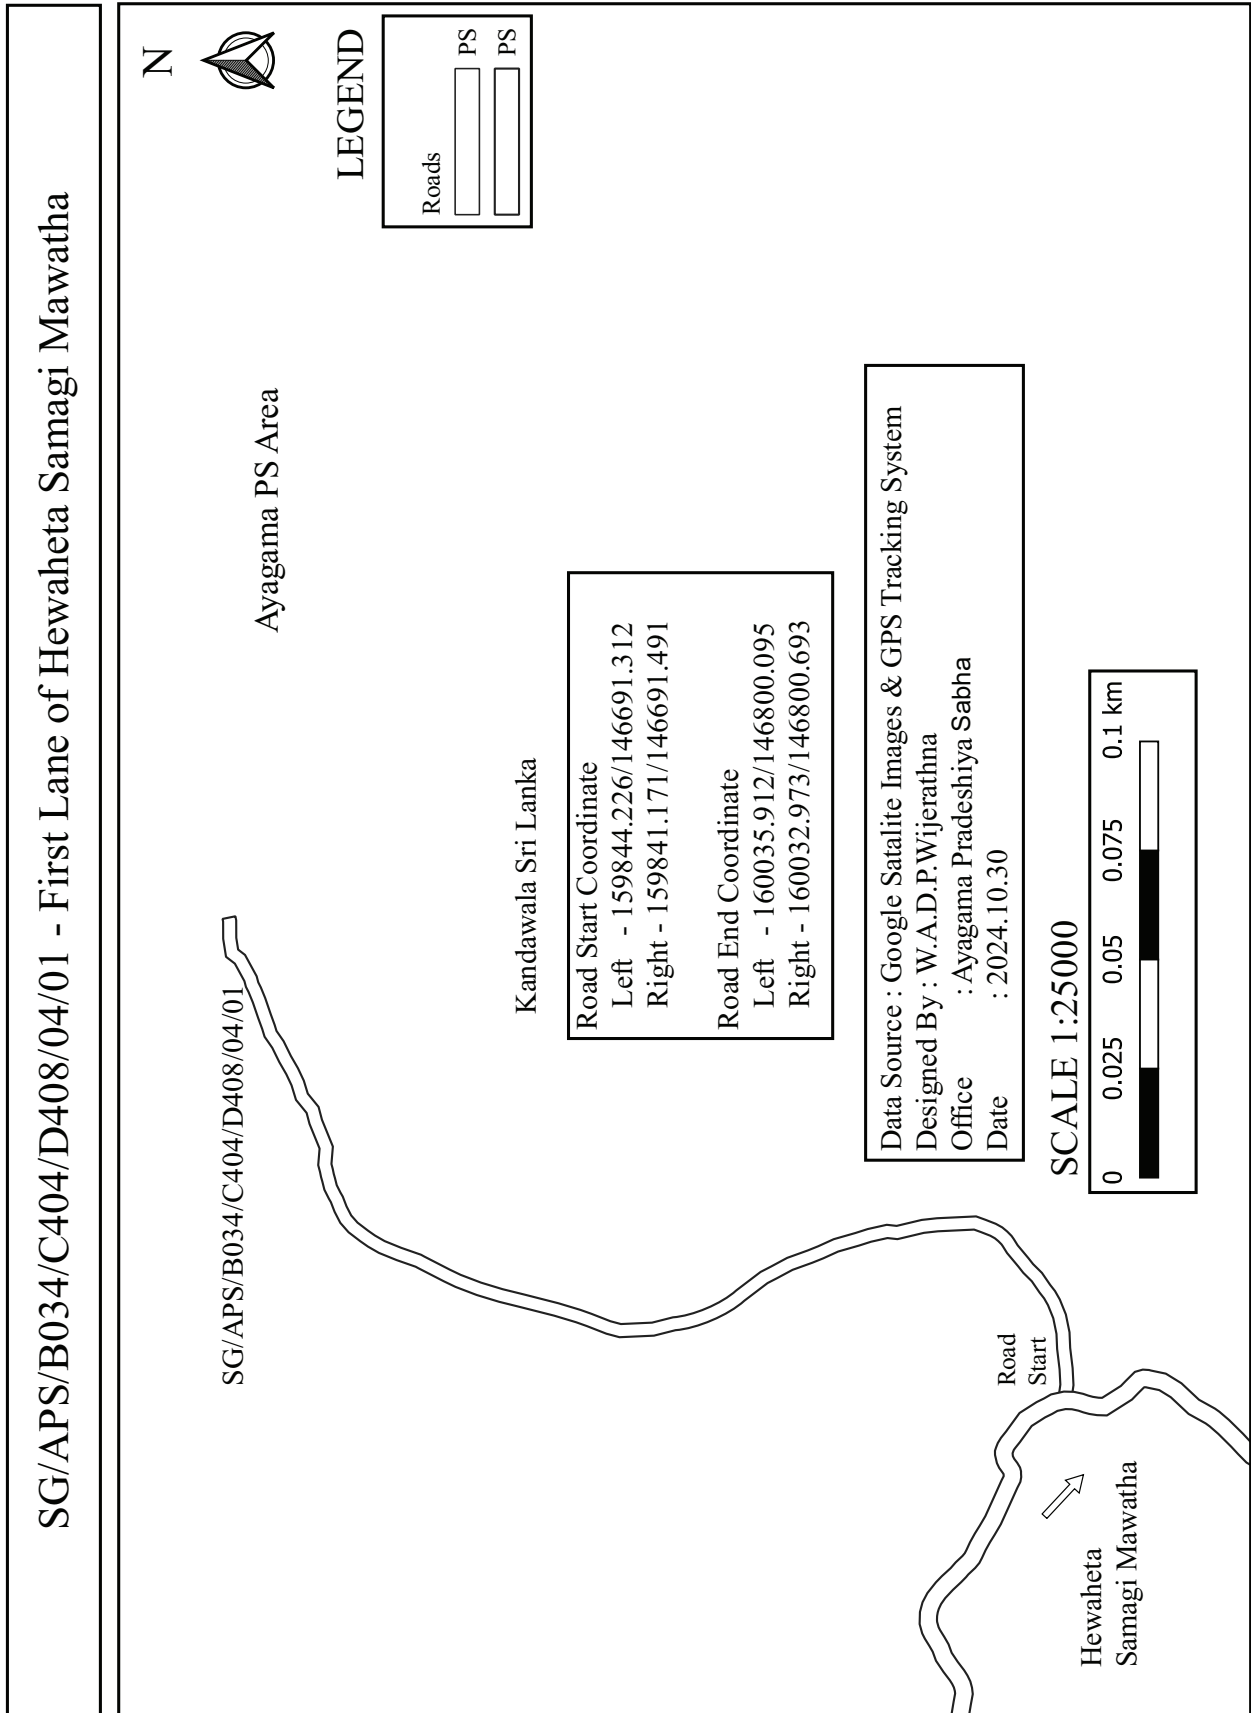


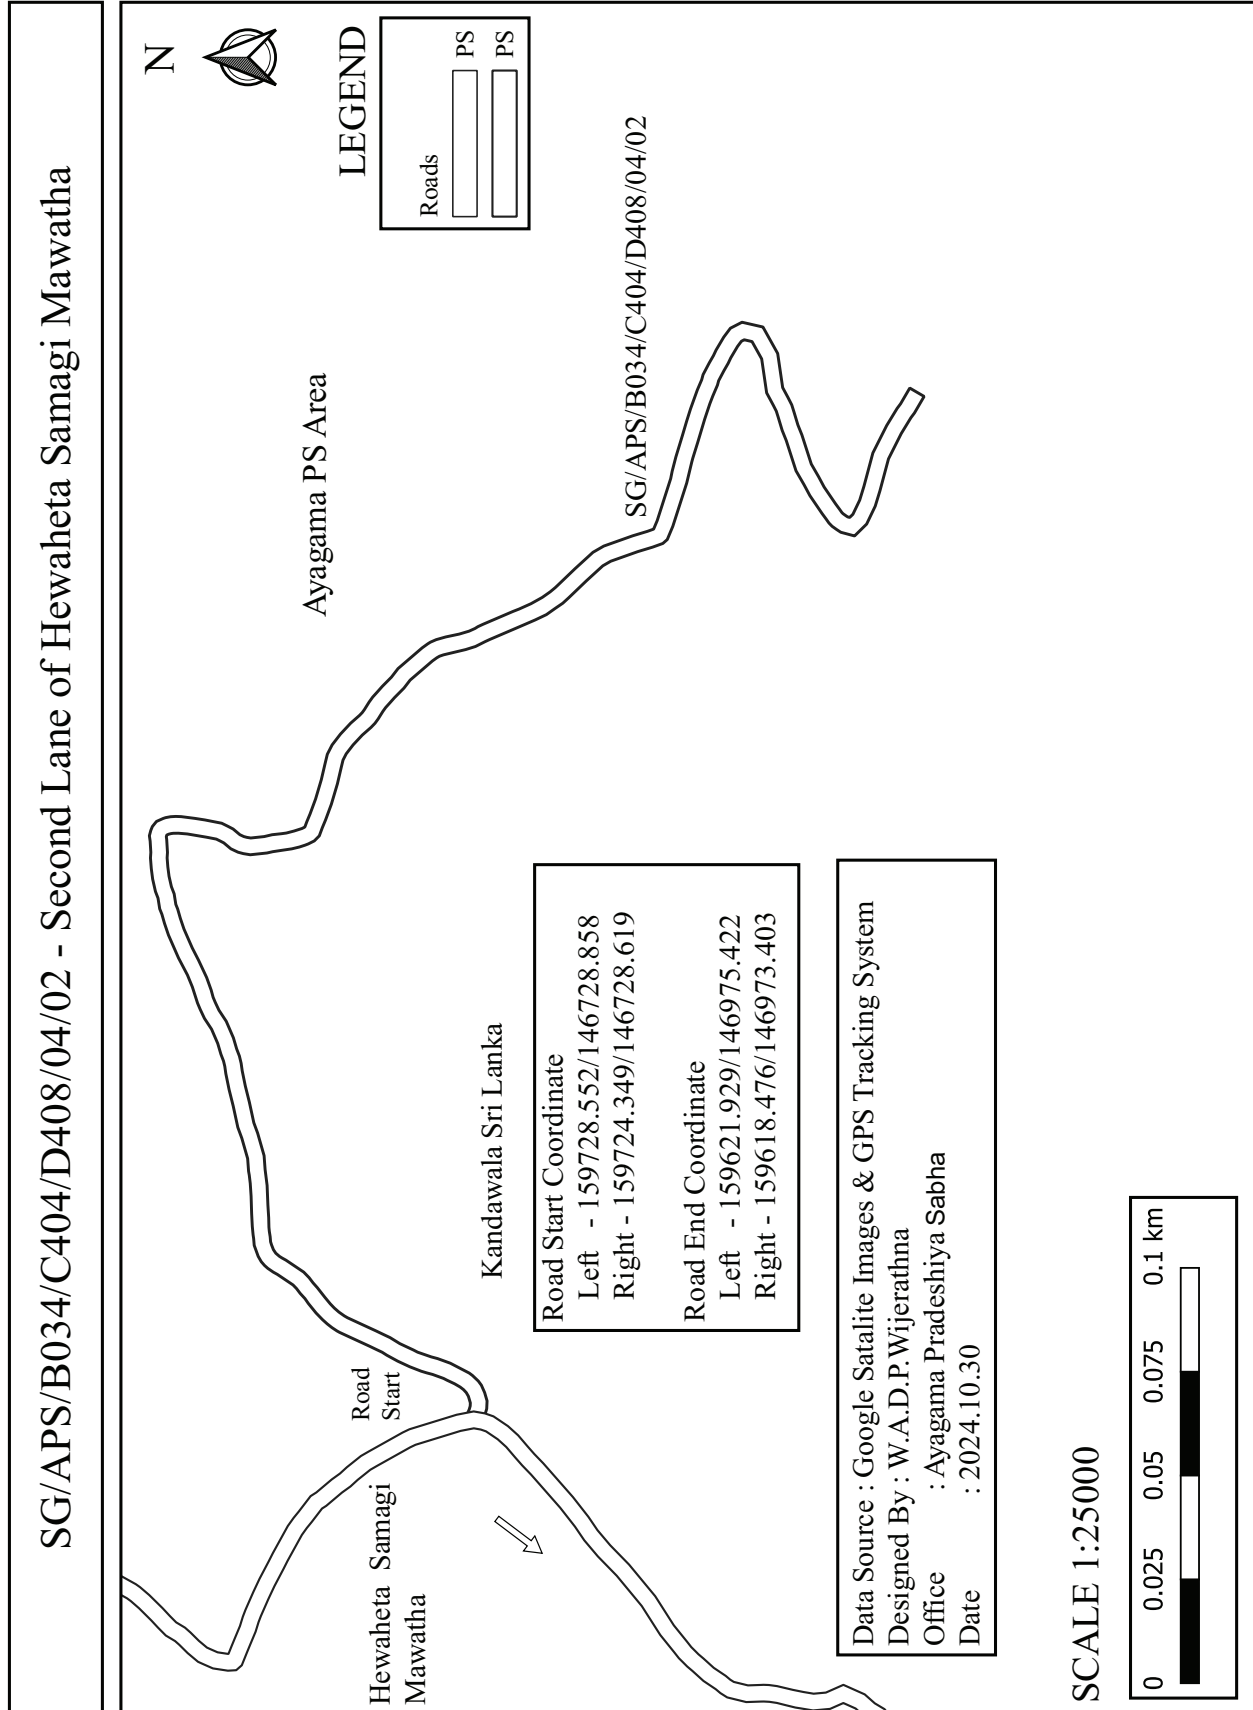



SG/APS/B034/C404/D408/04/02/01 - Footpath - First By Pass Way of Second Lane of Hewaheta
Samagi Mawatha

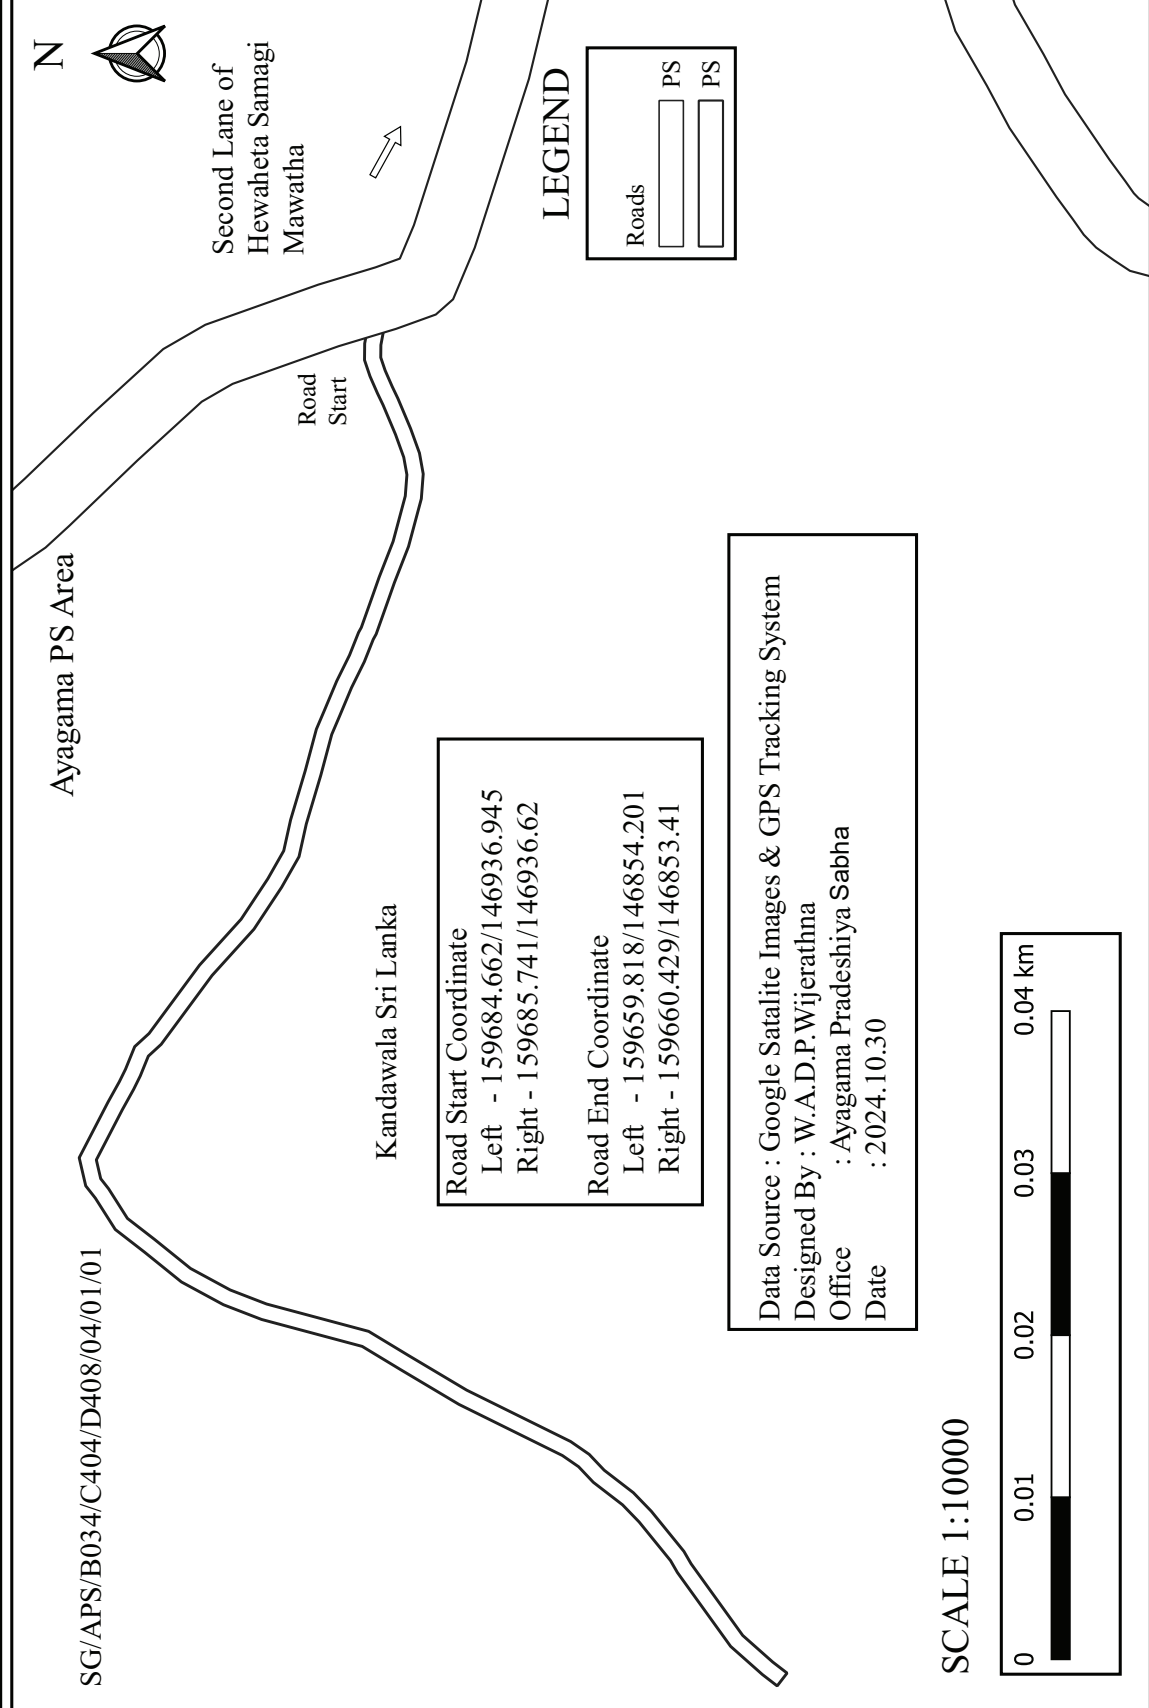


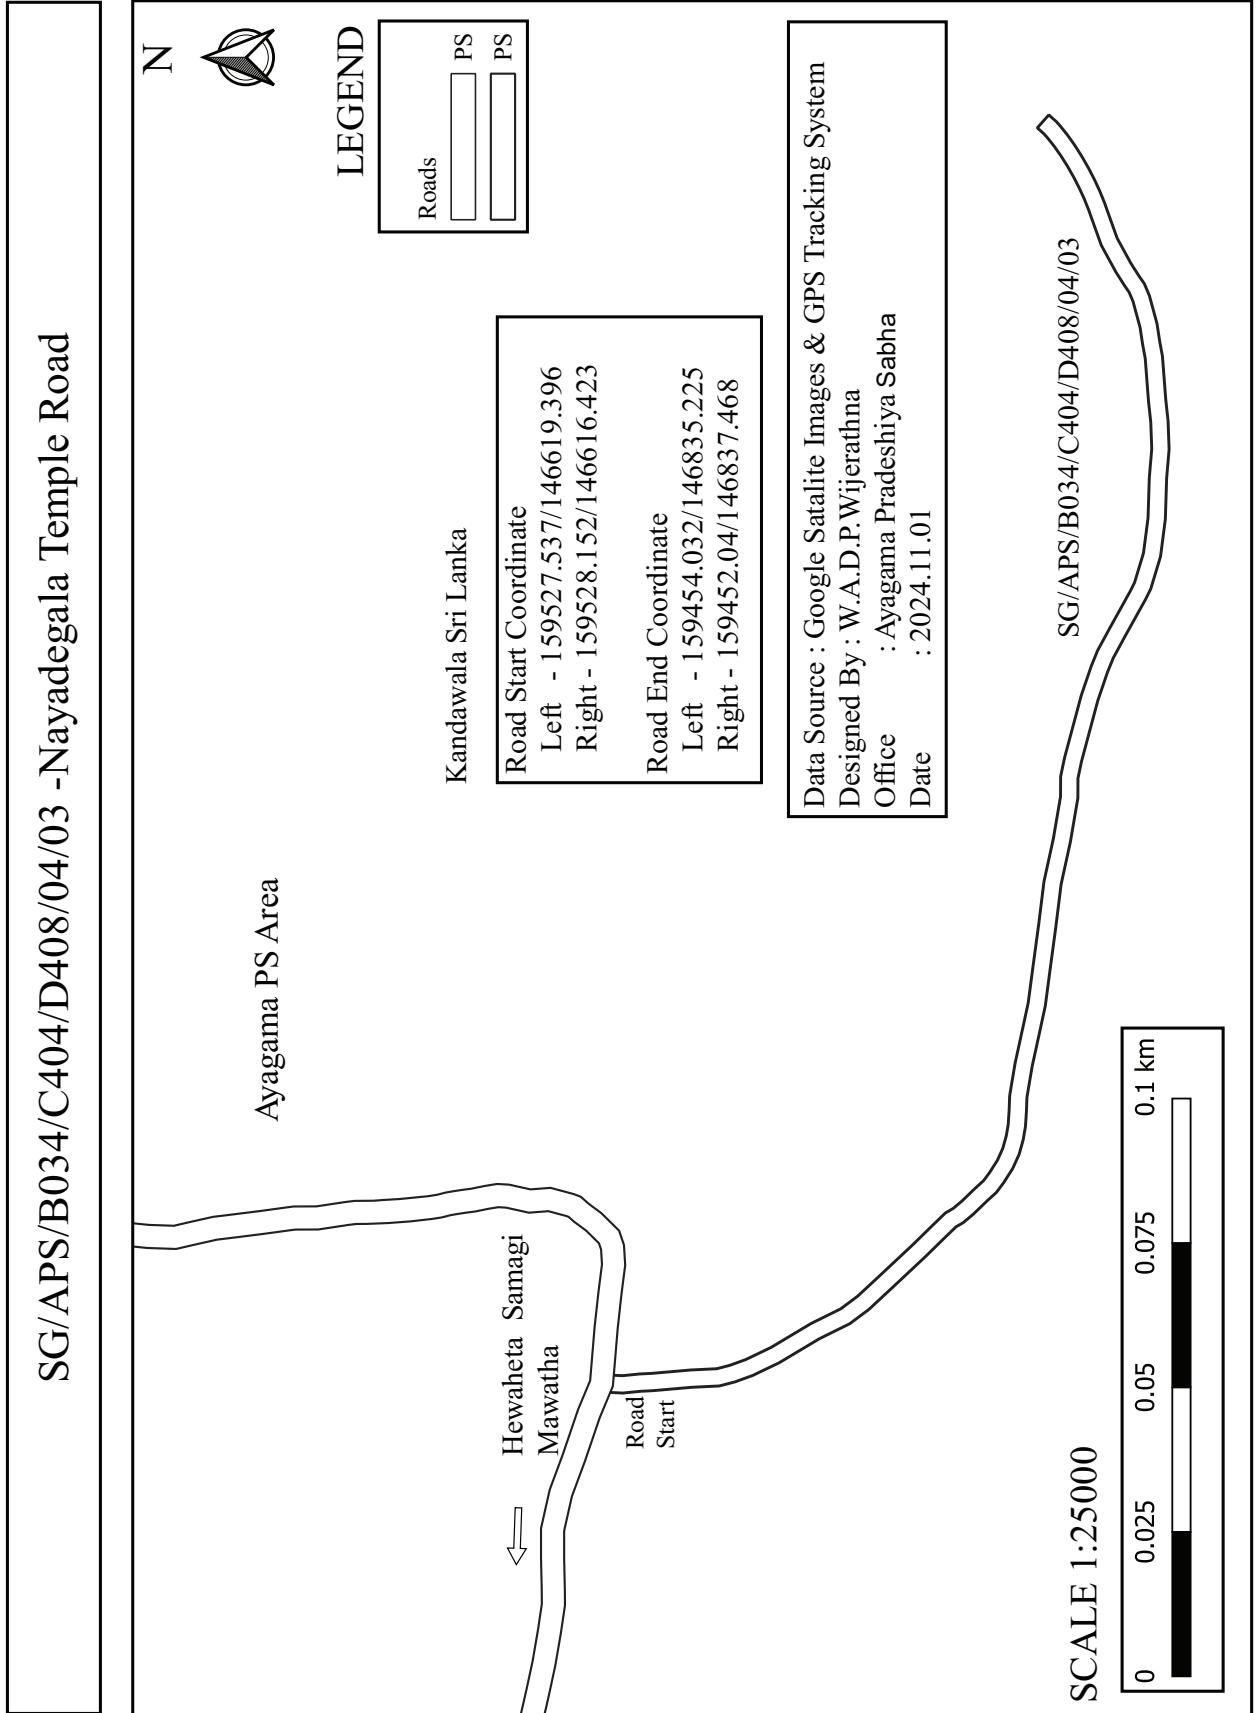

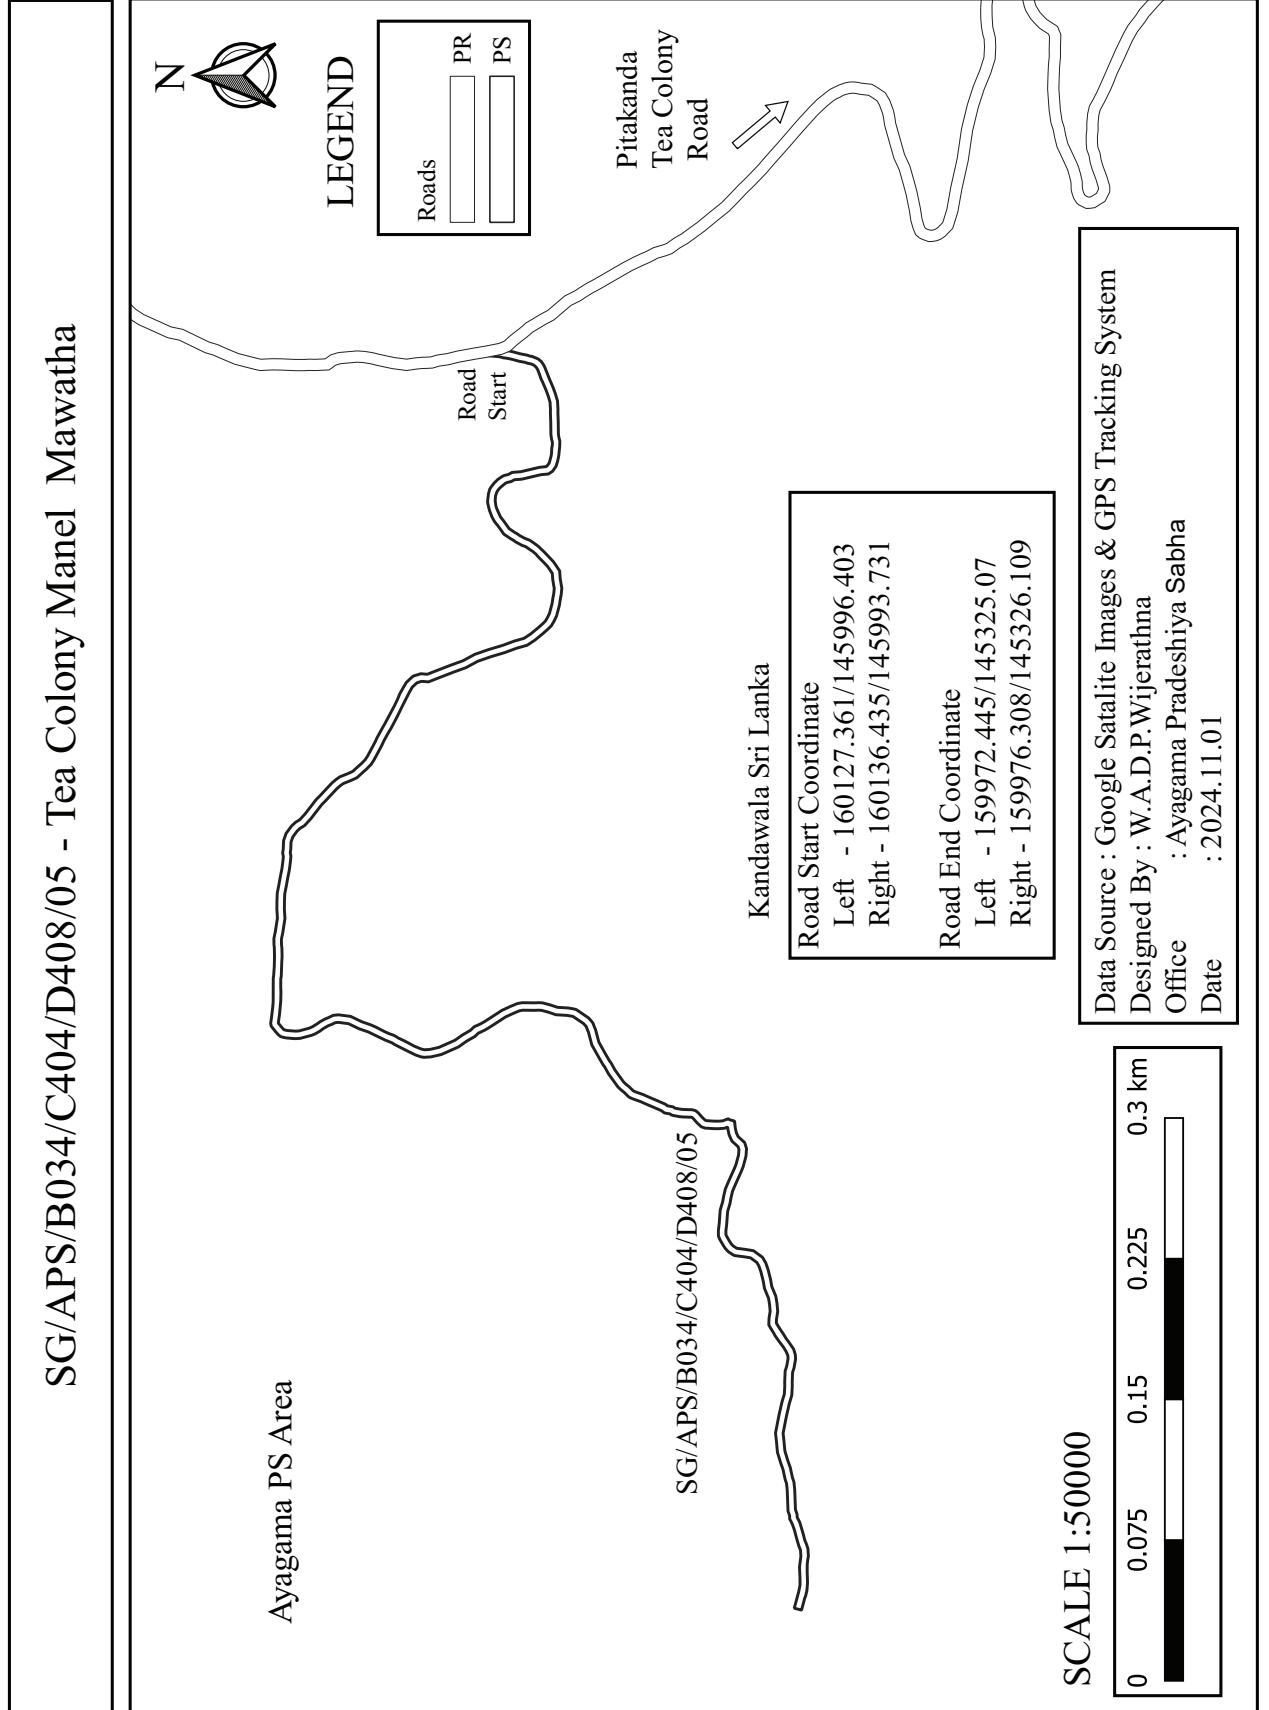


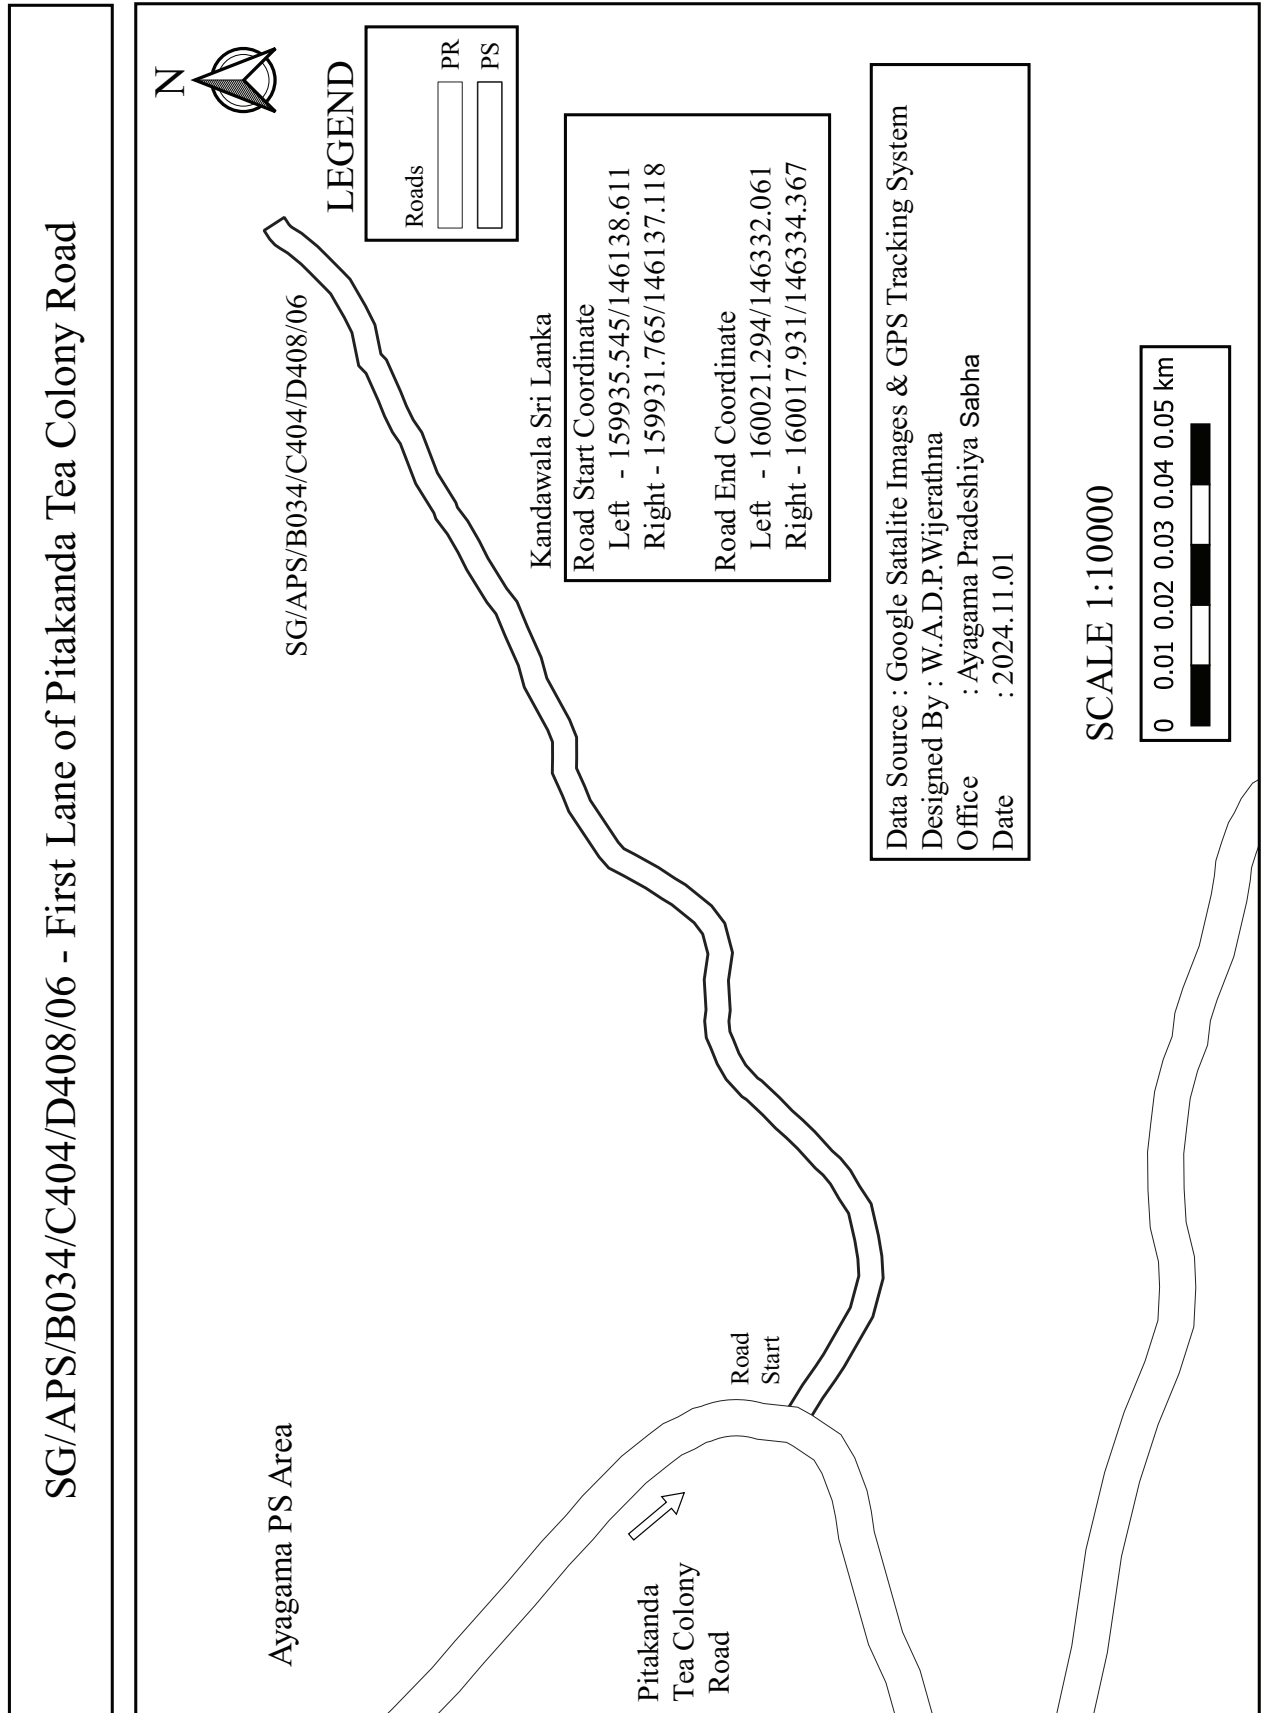

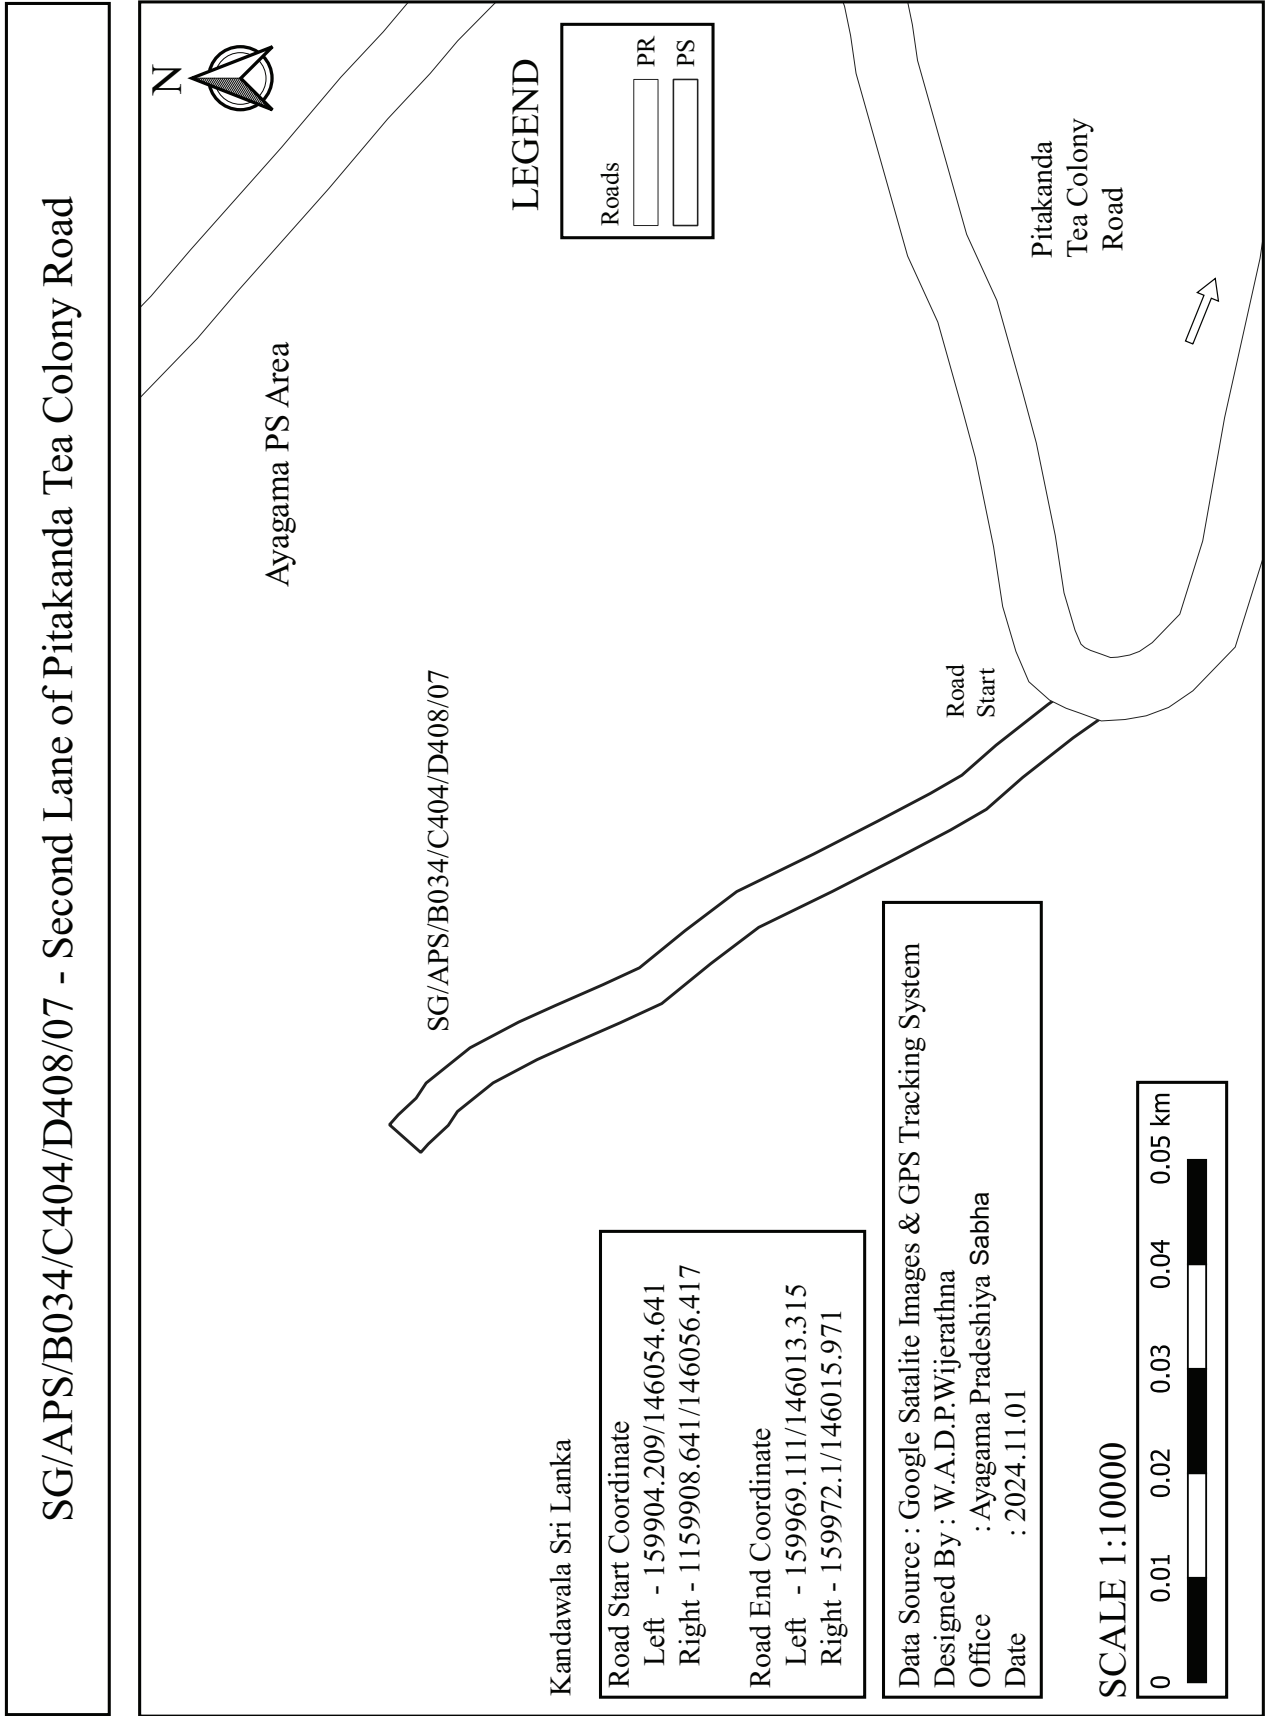


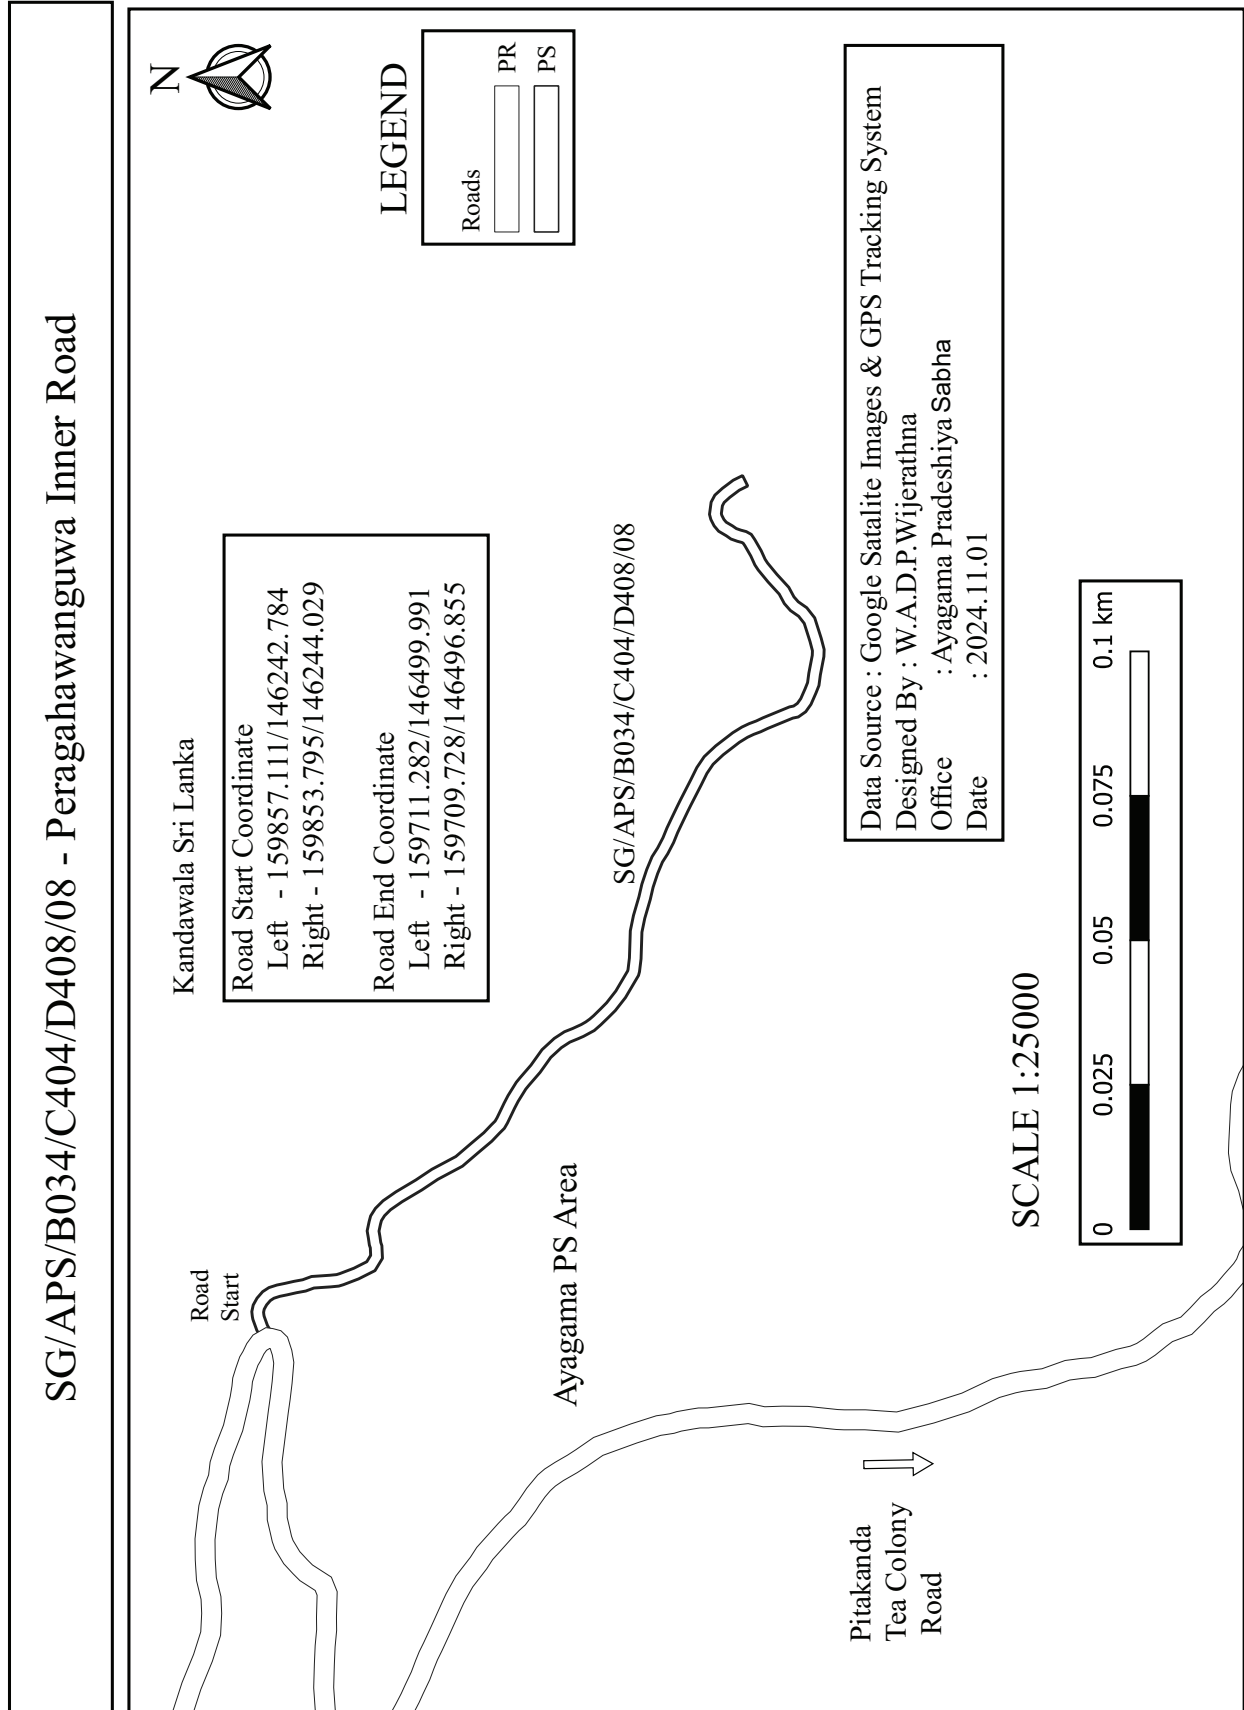



SG/APS/B034/C404/D408/09 - Tea Colony Divigalpoththa Road

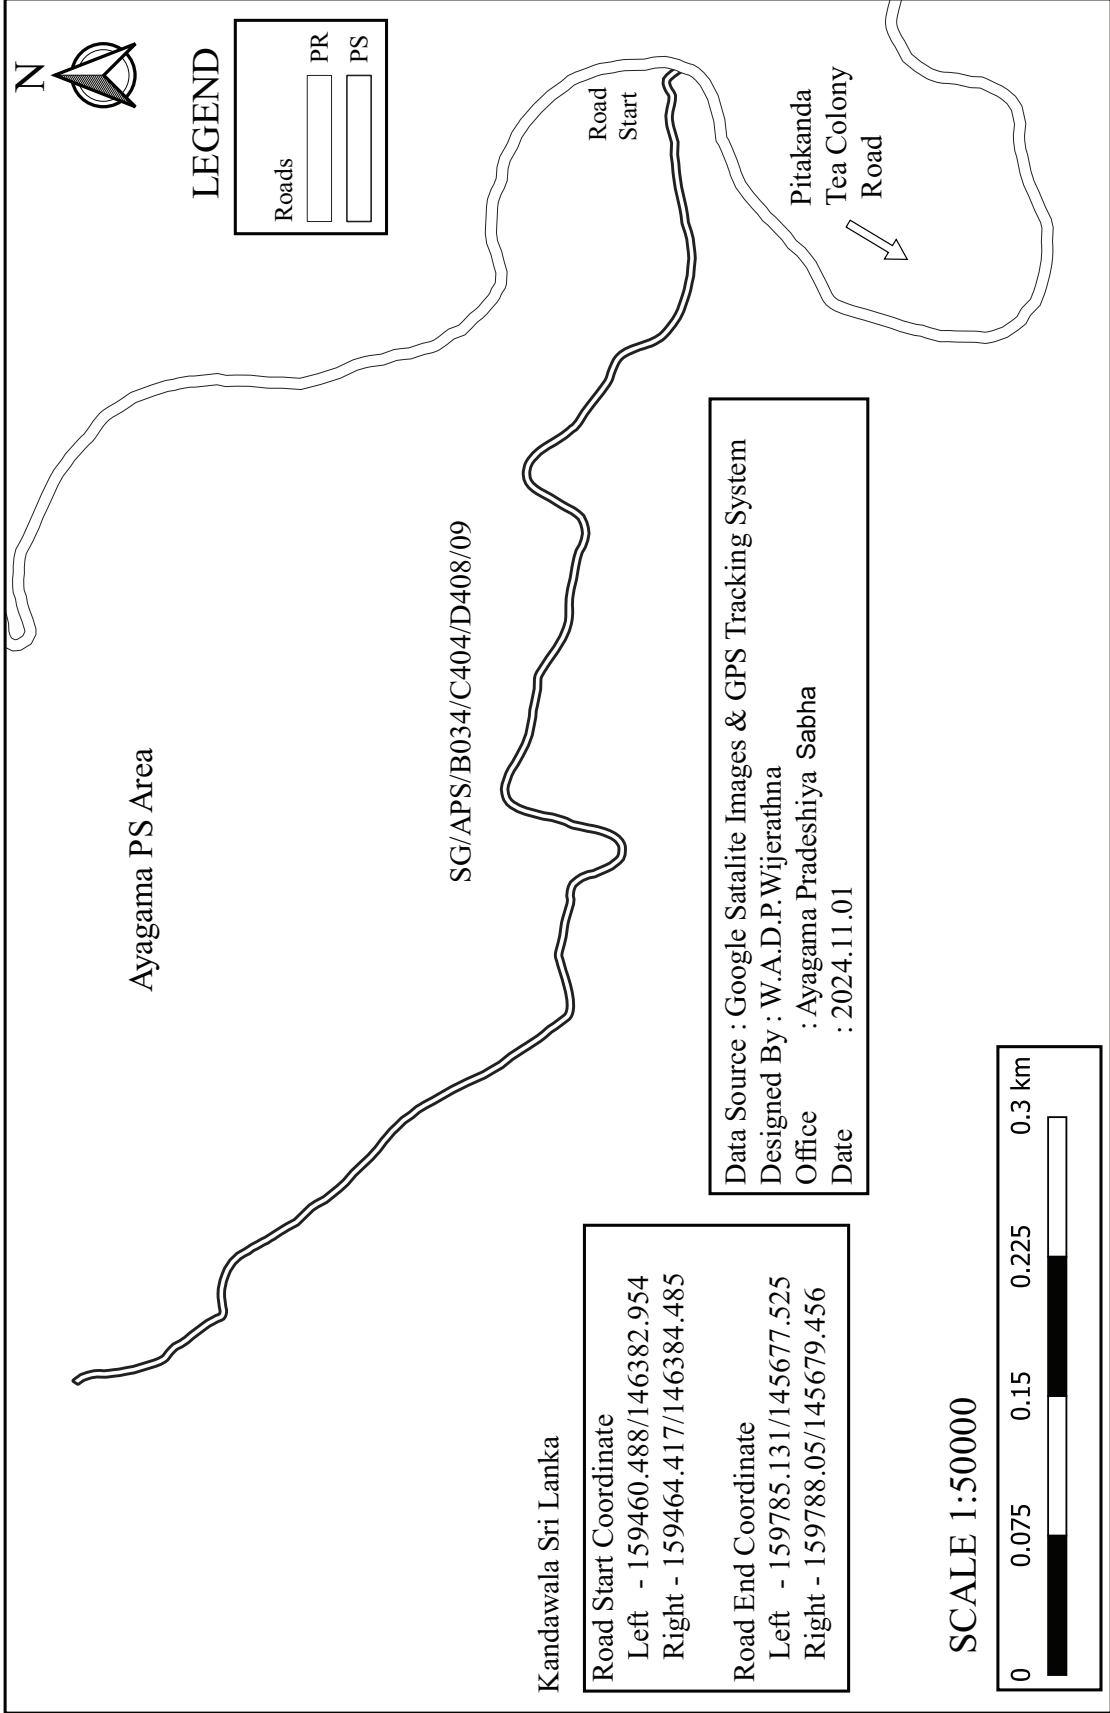


SG/APS/B034/C404/D408/10 - Tea Colony Batahena Road

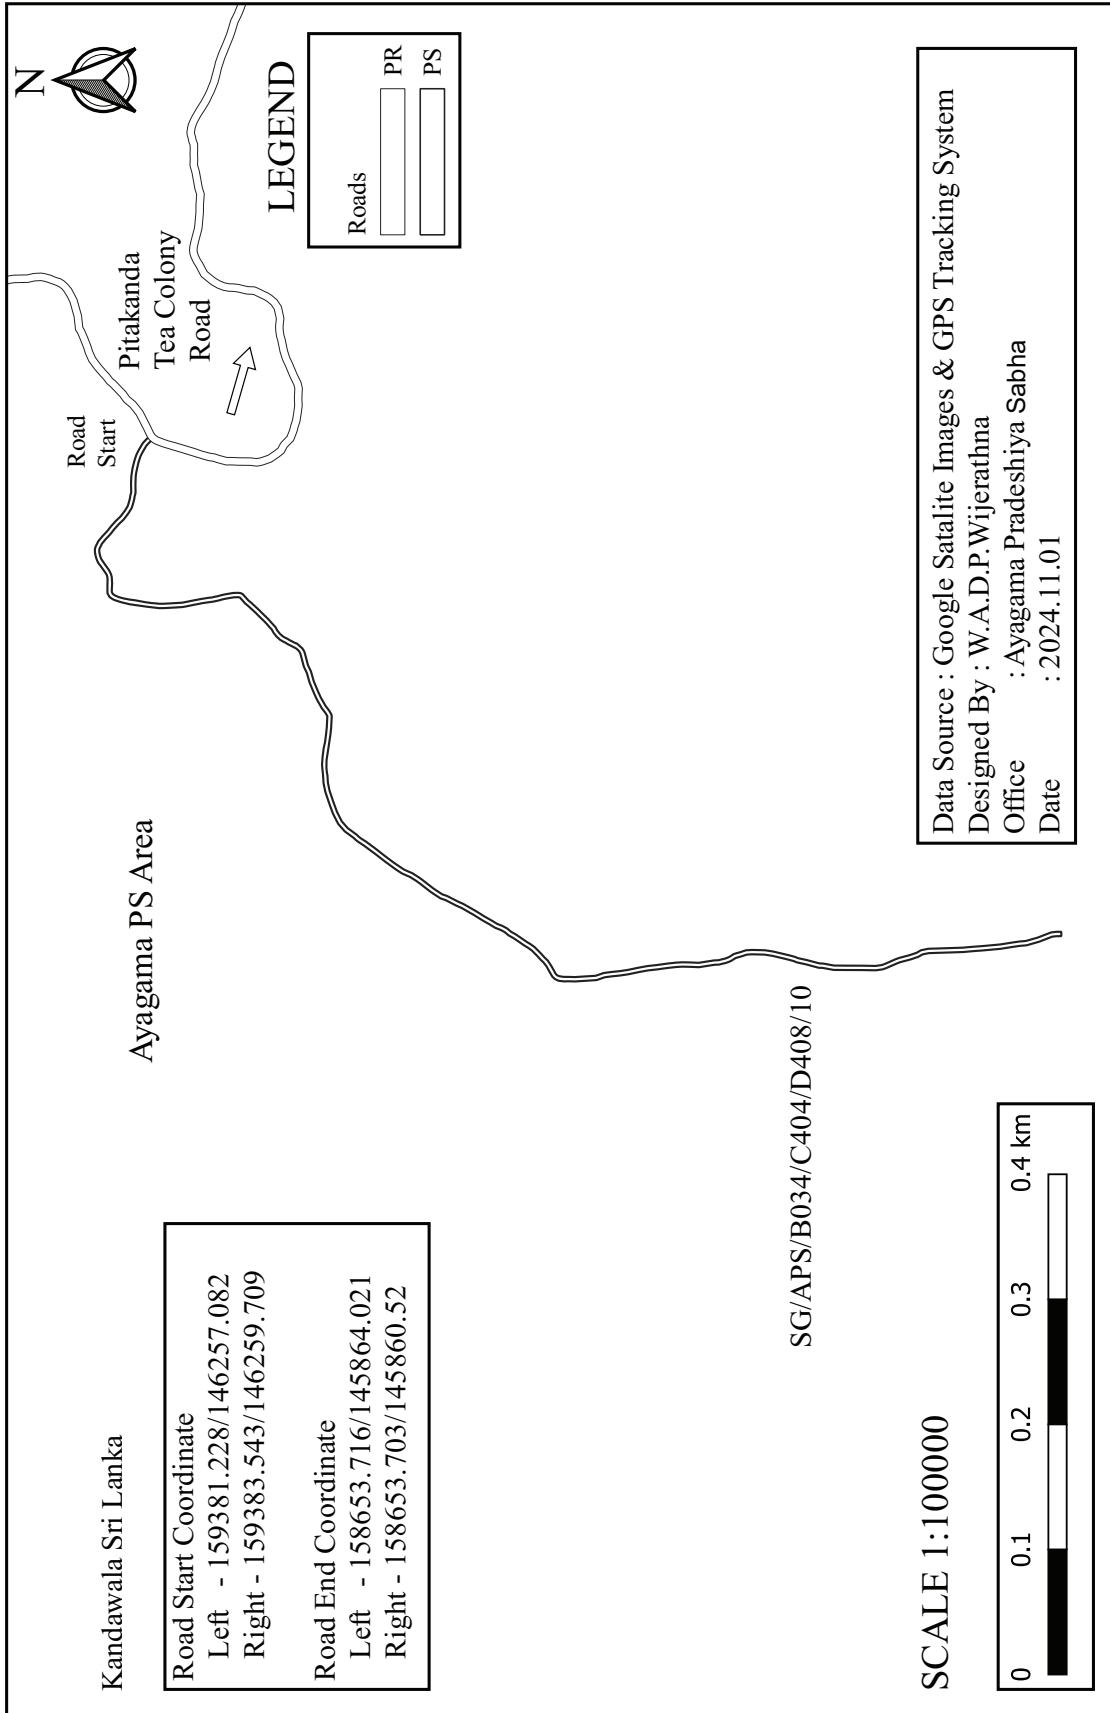


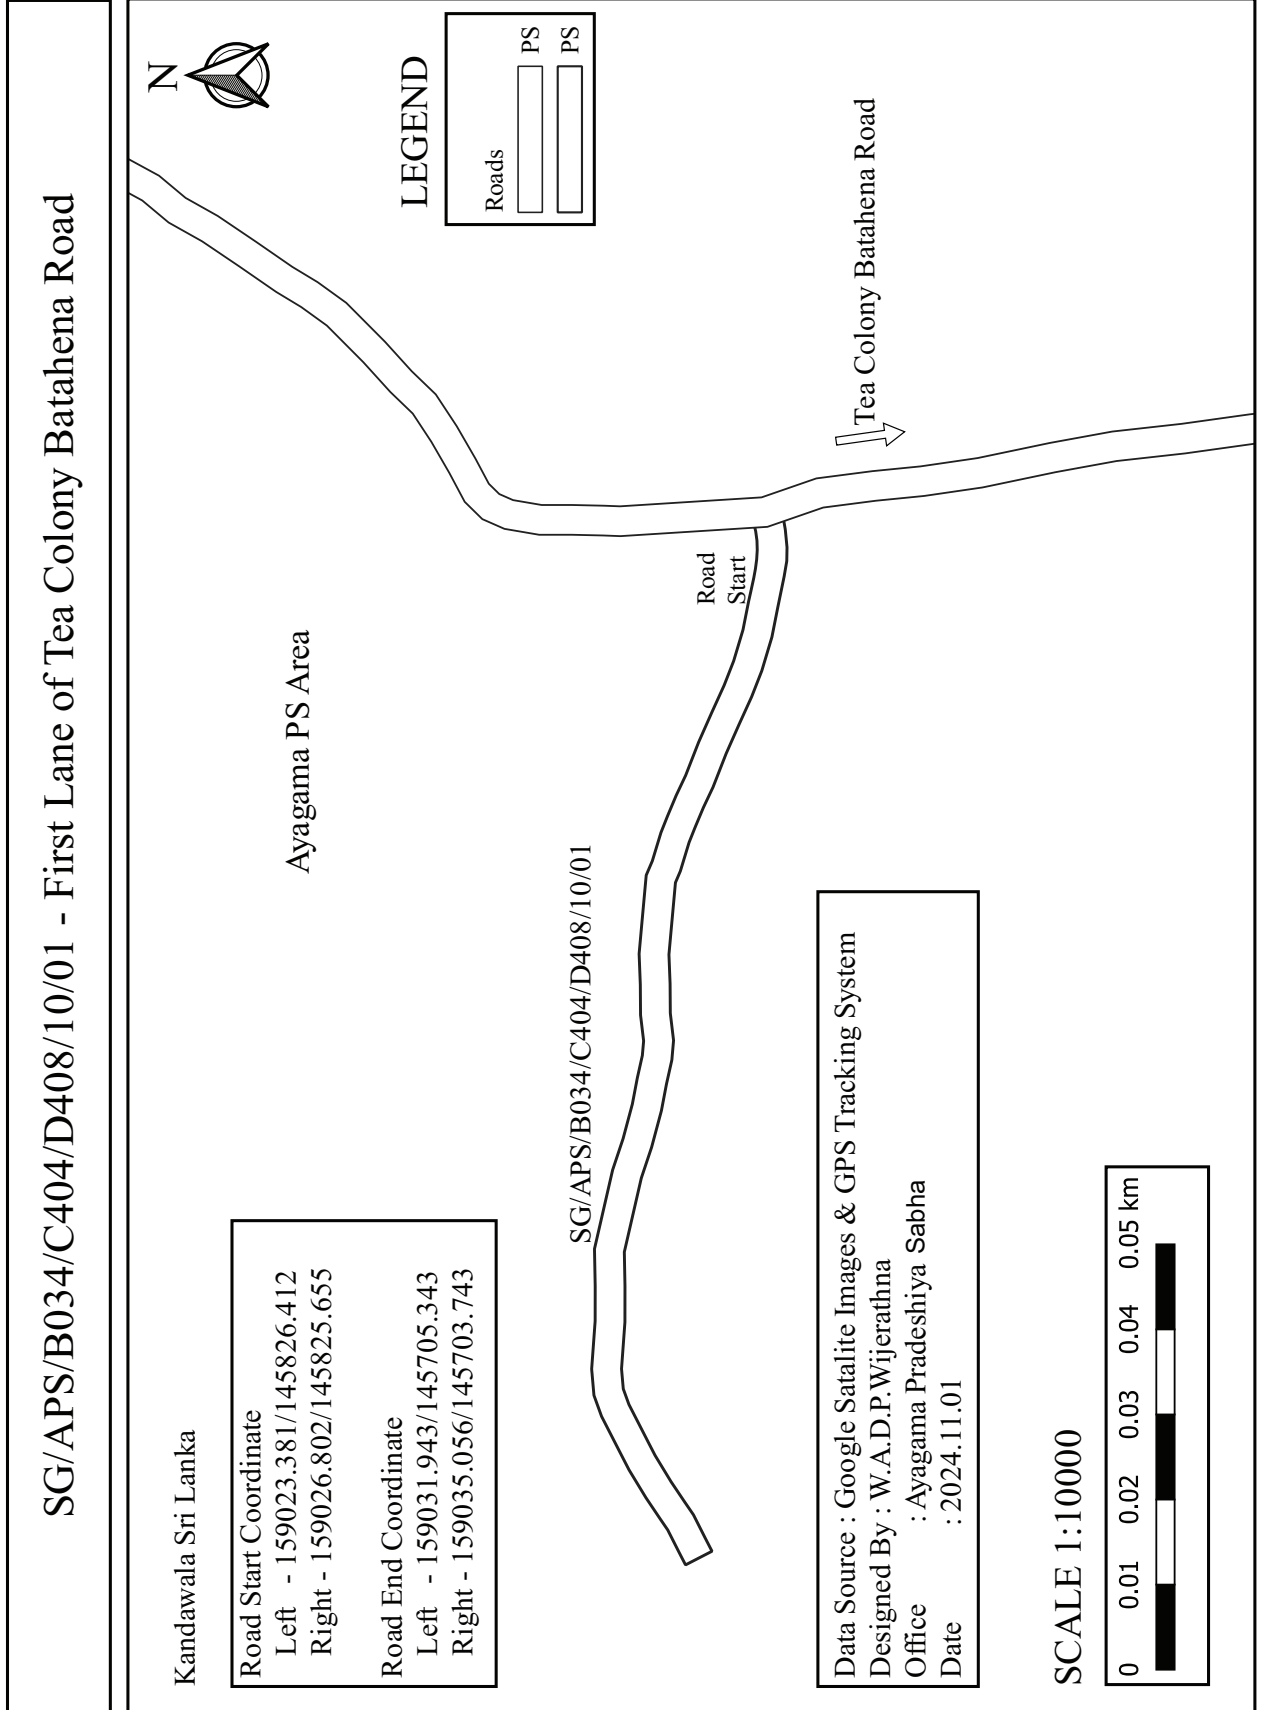


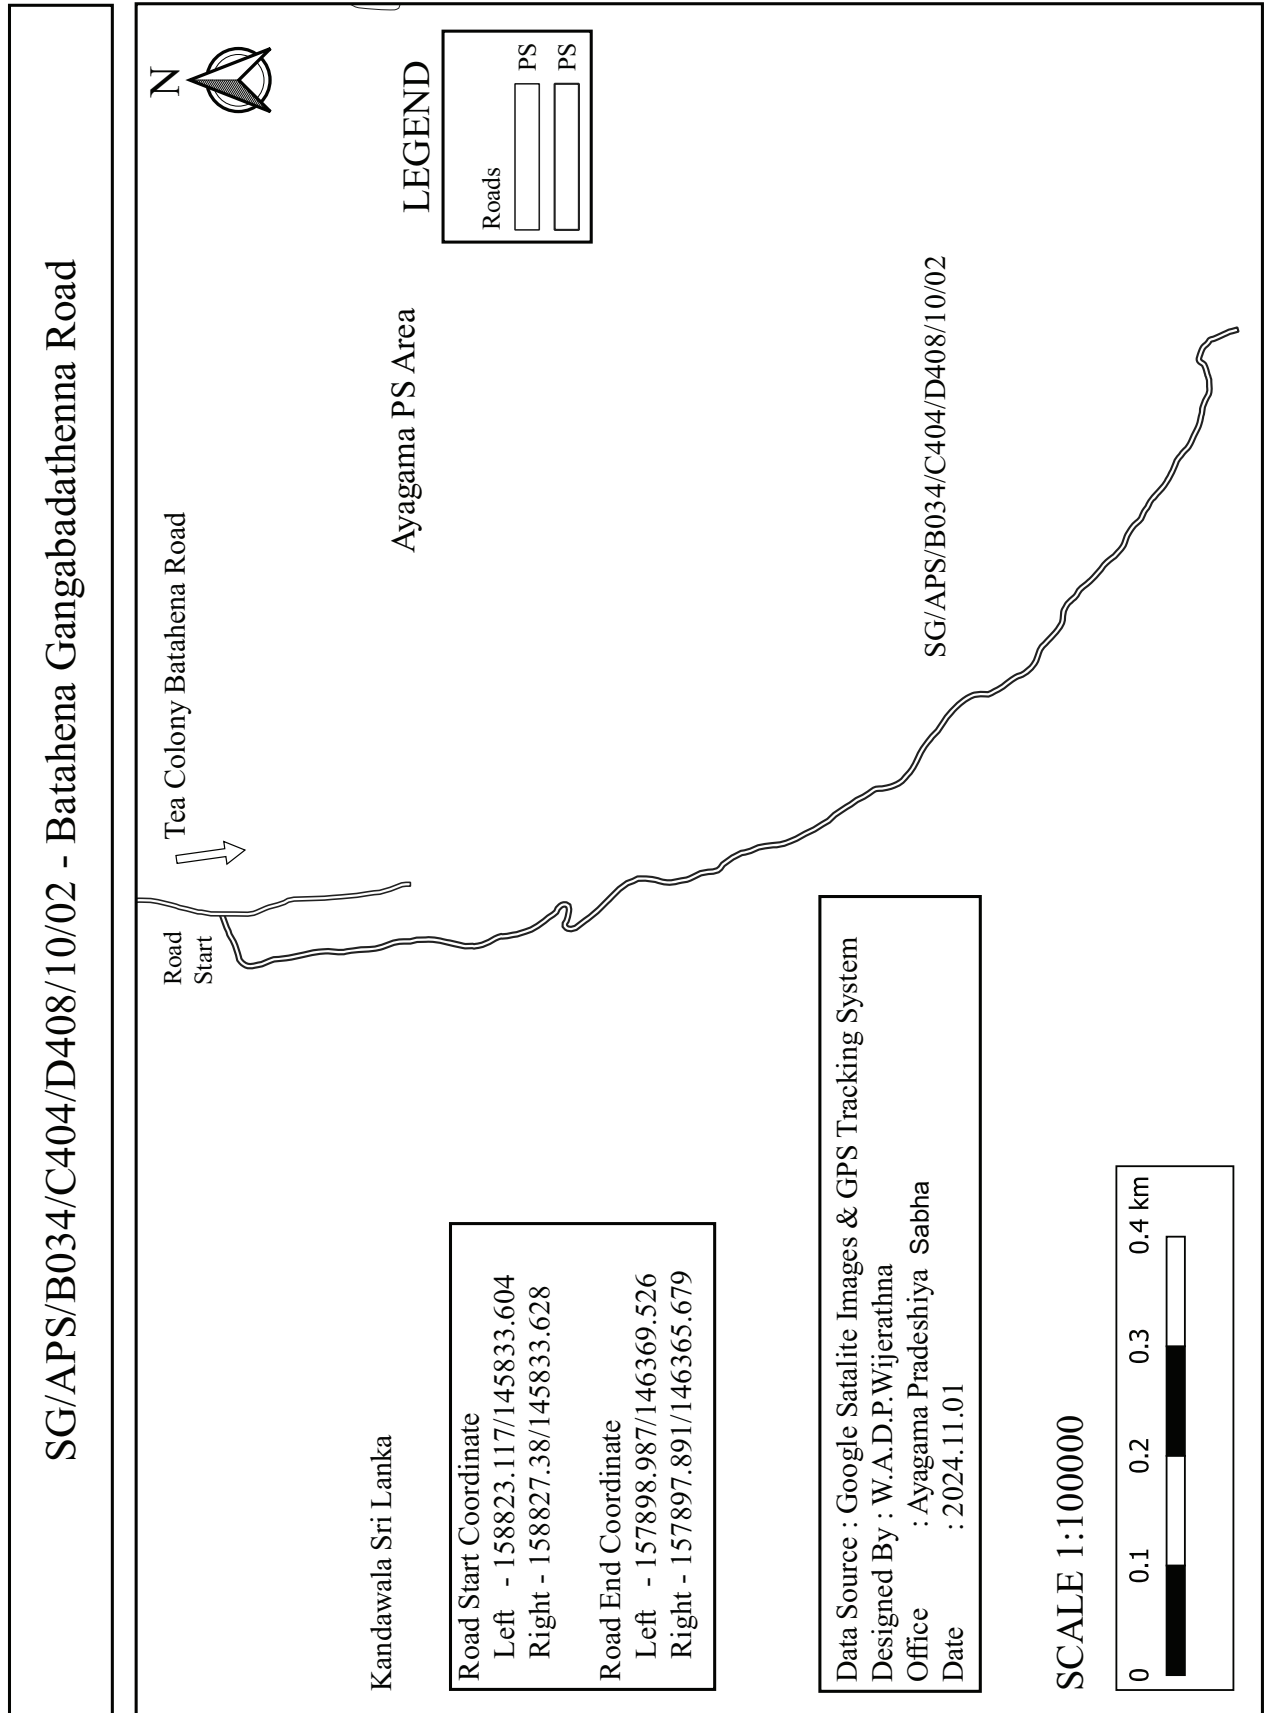

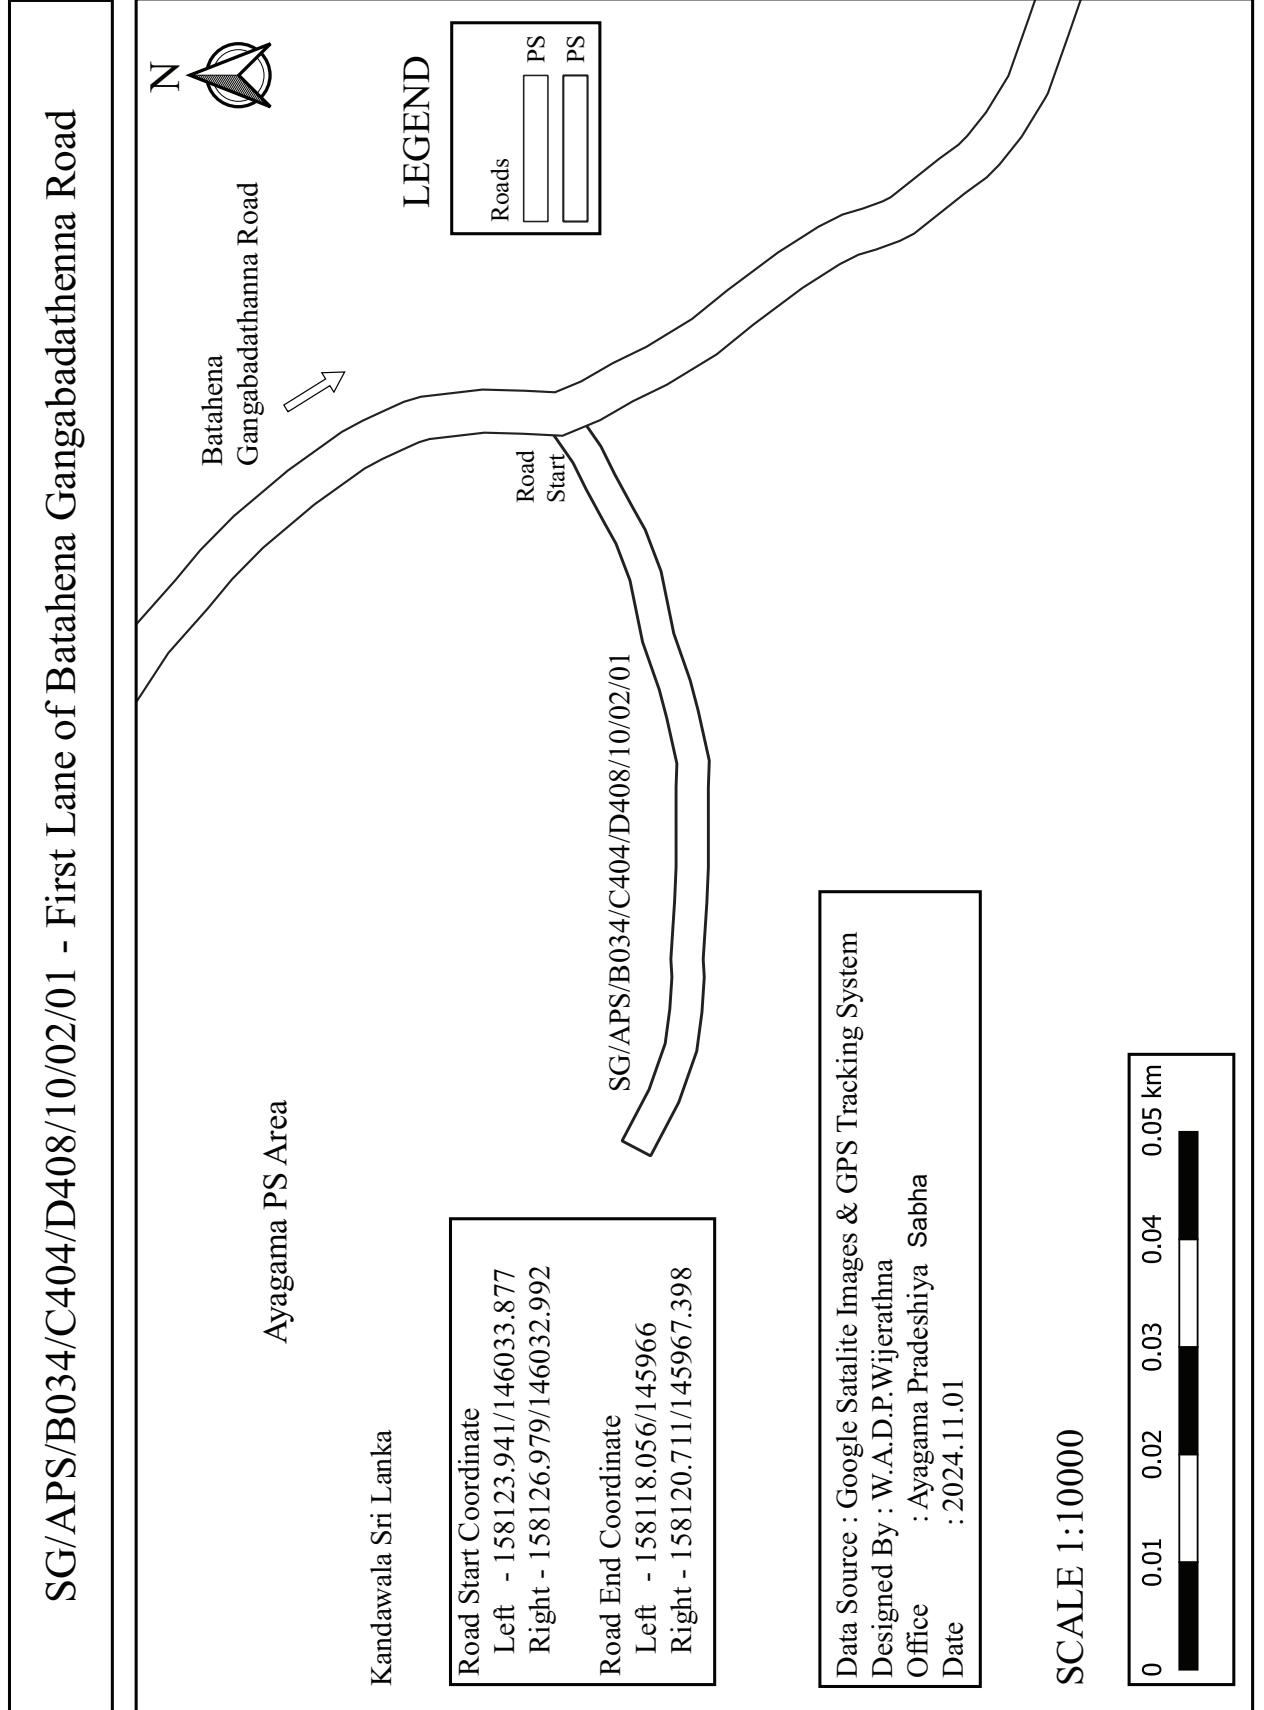



SG/APS/B034/C404/D408/10/03 - Batahena Panwilathenna Road

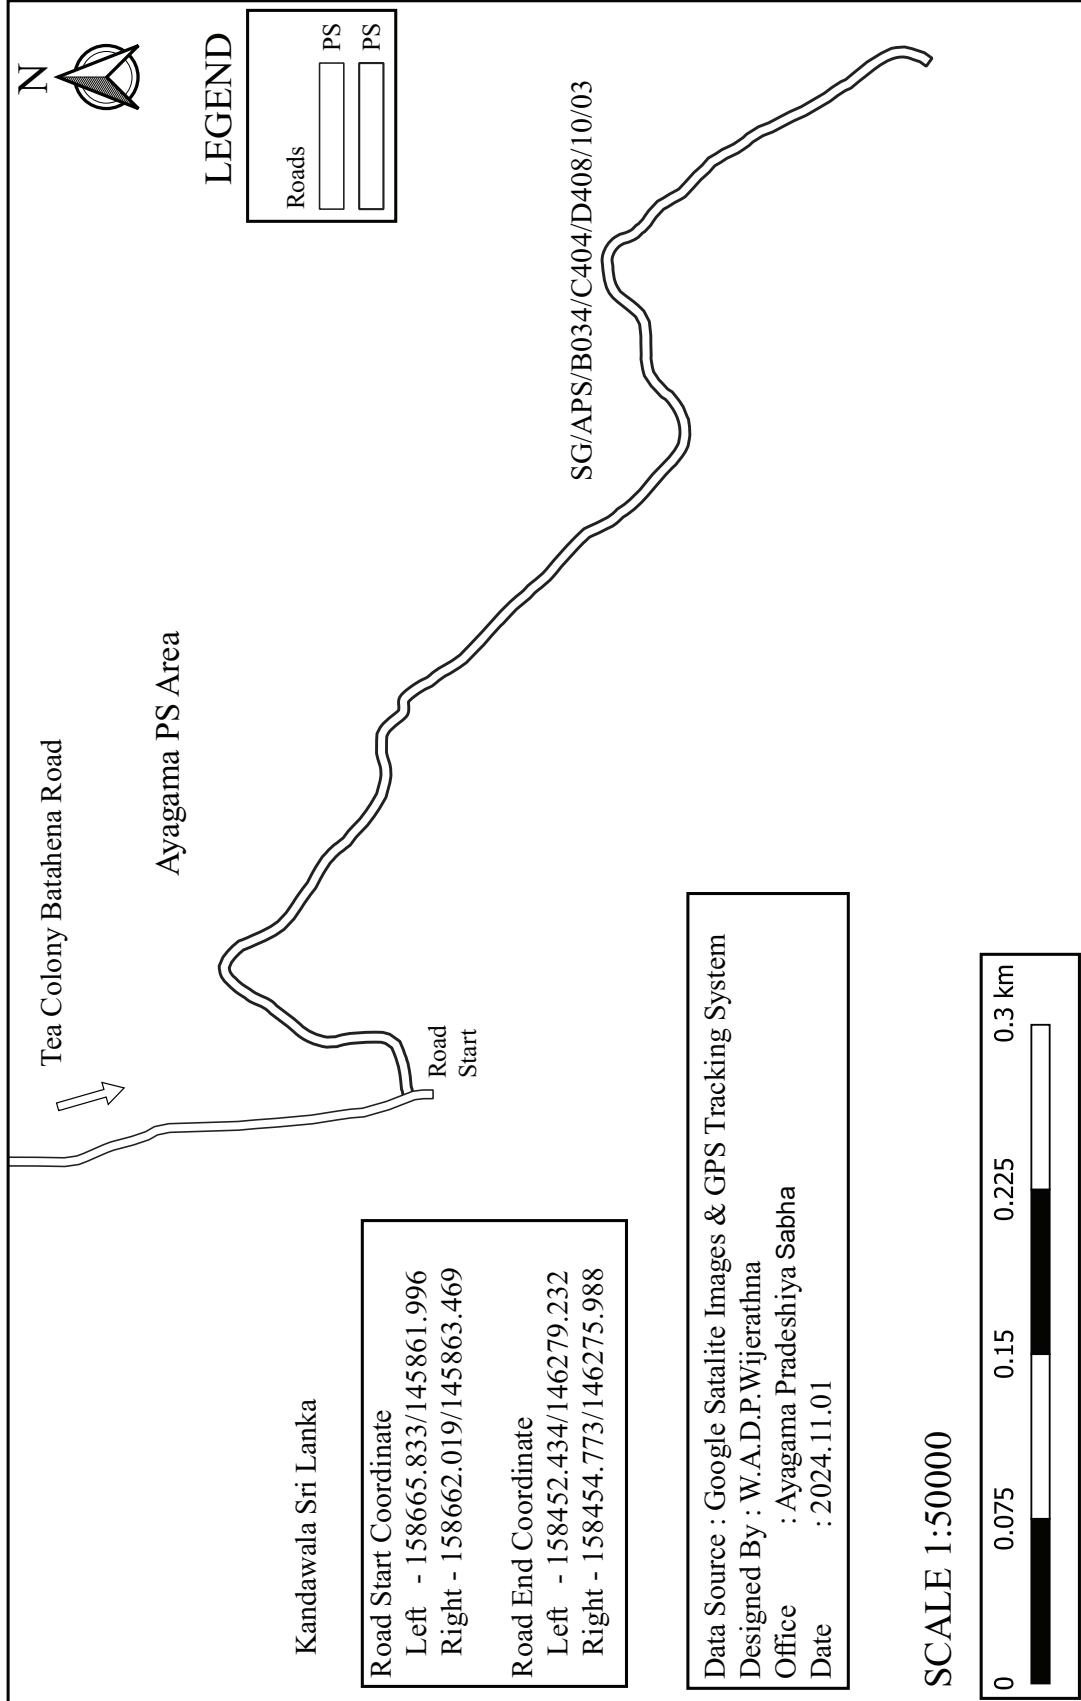


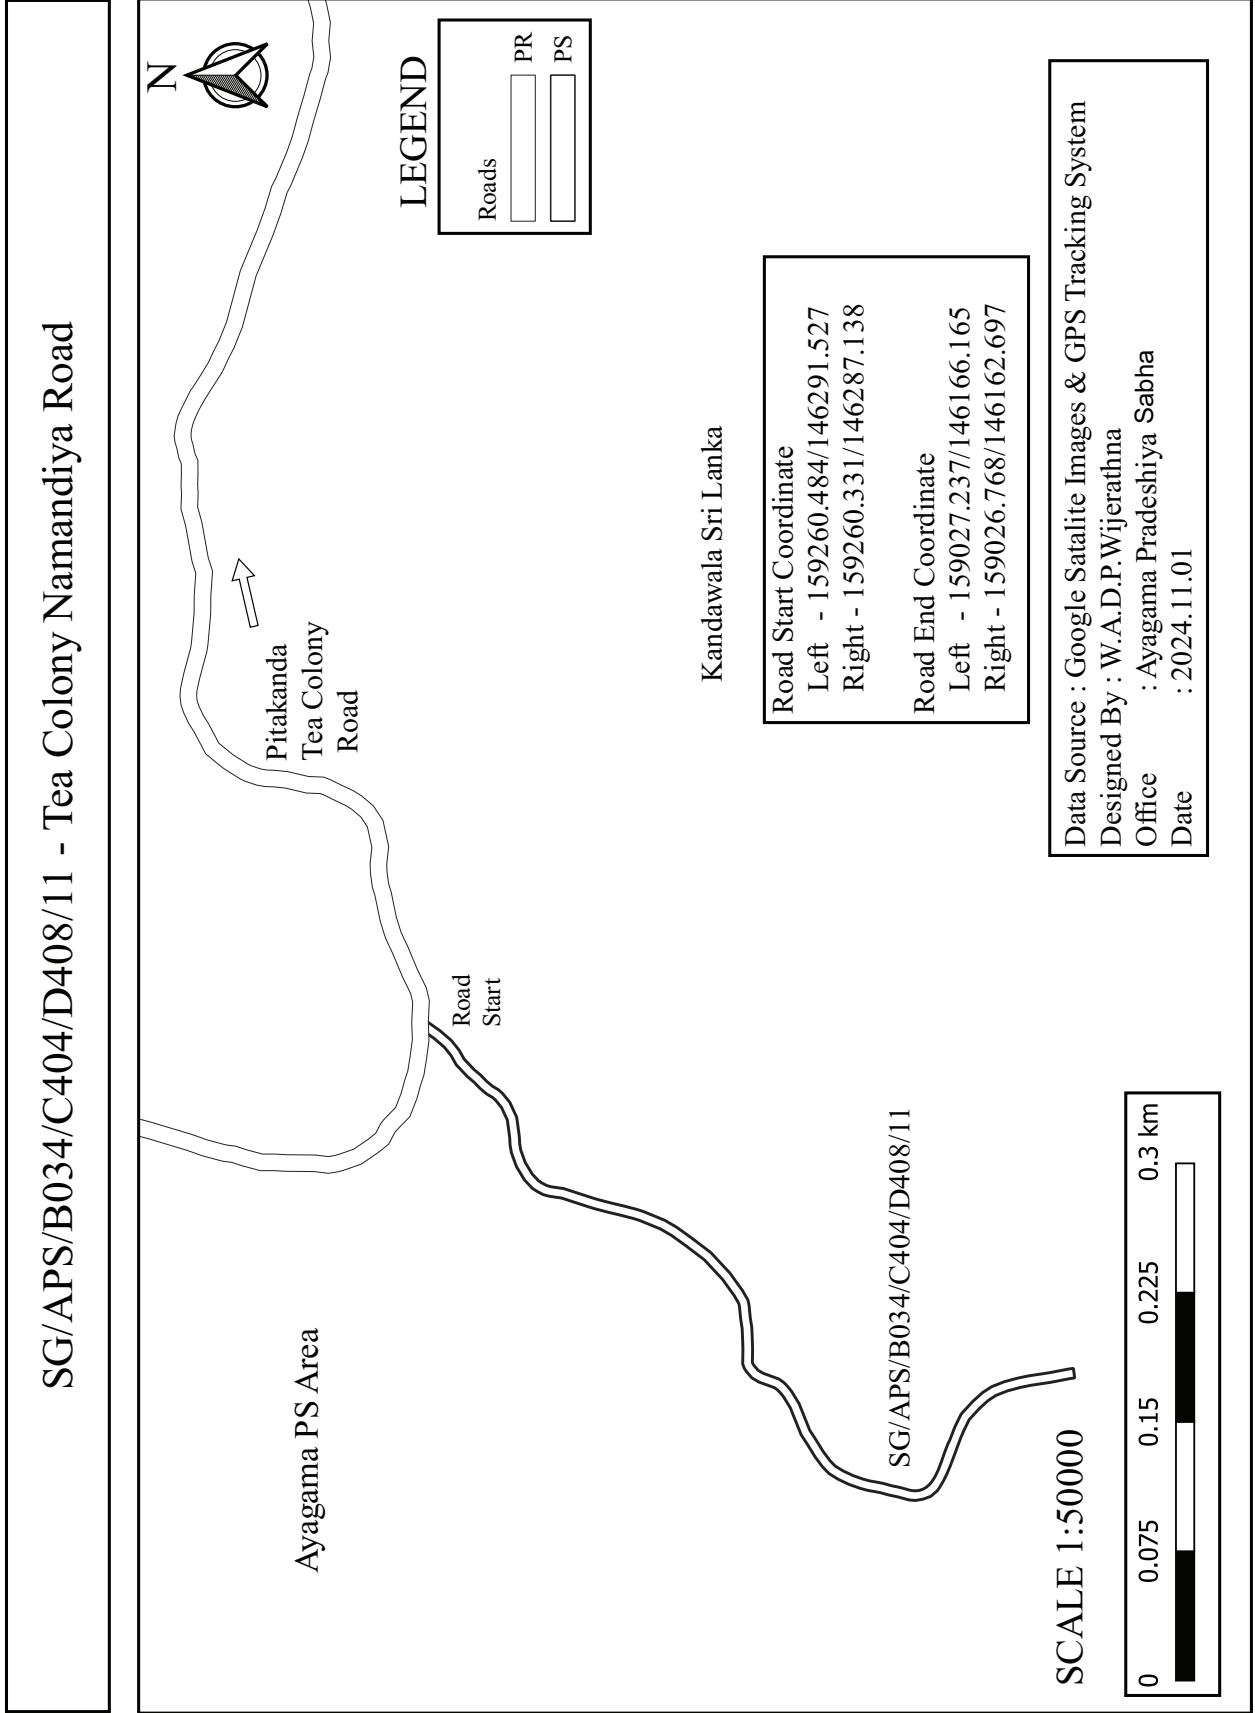


SG/APS/B034/C404/D408/12 - Kanduruwandola Galapalla Road

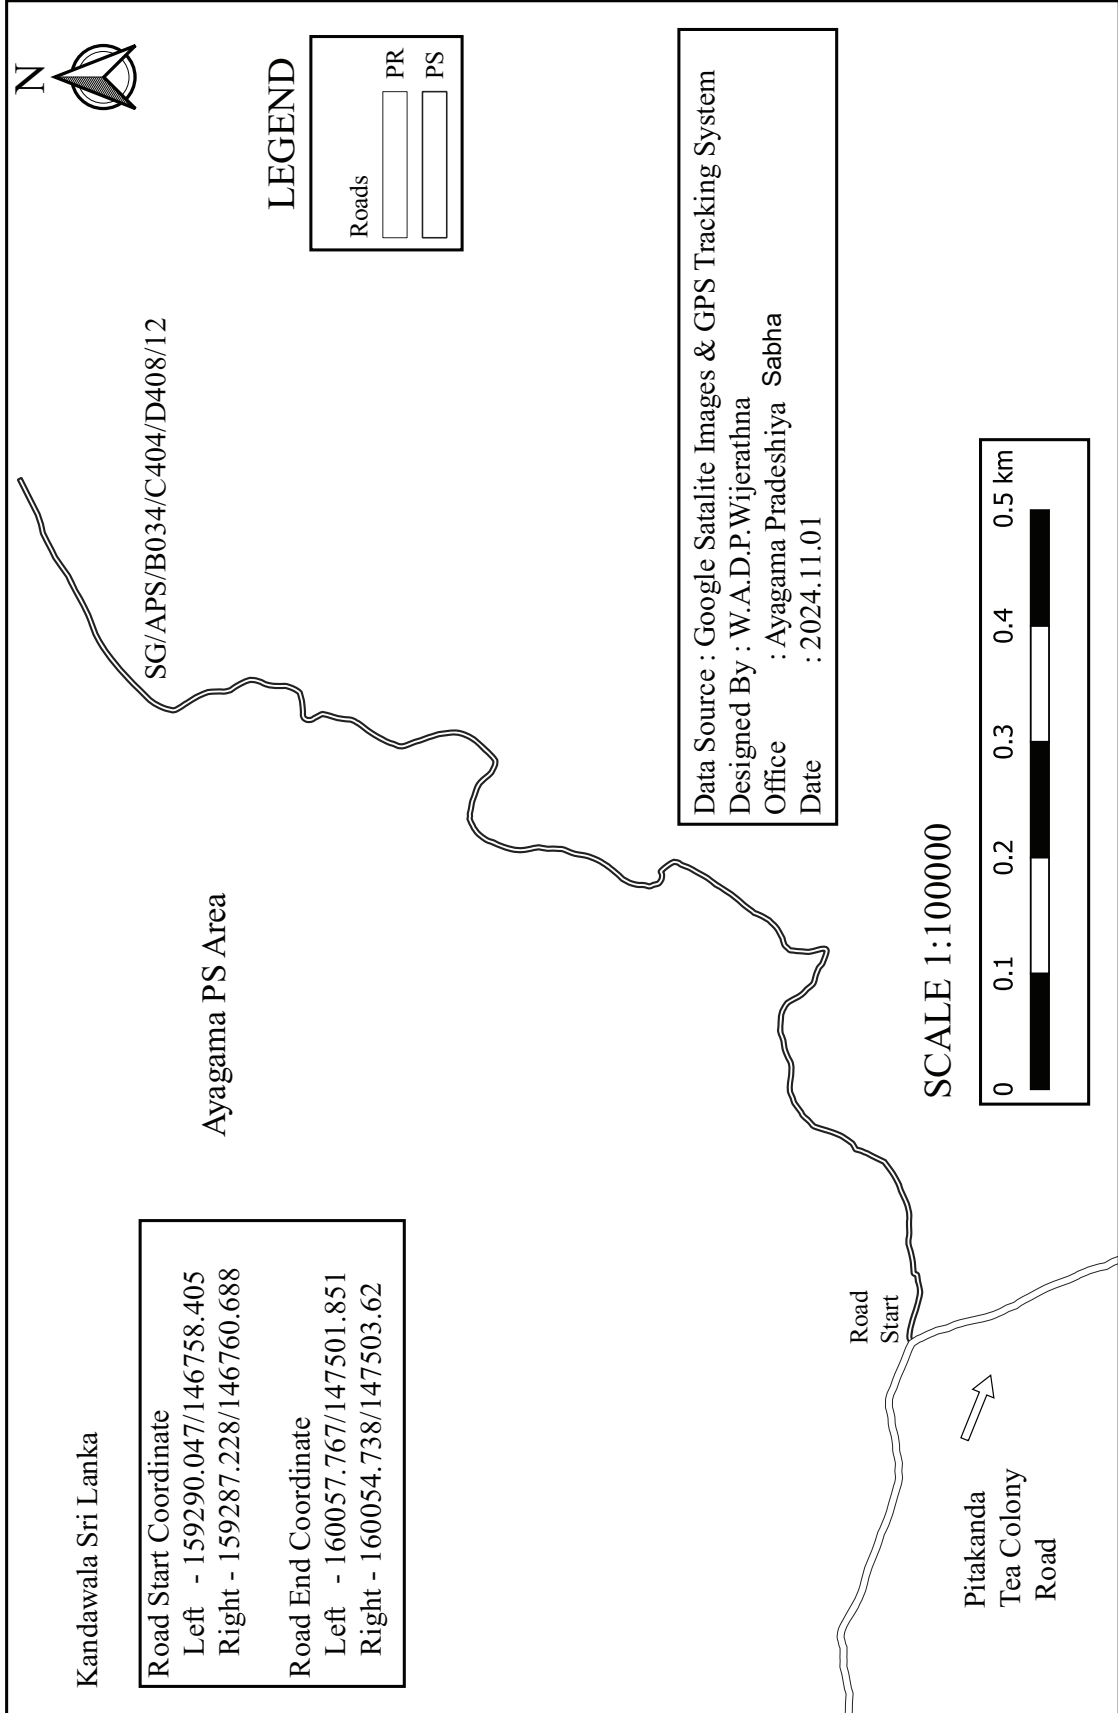


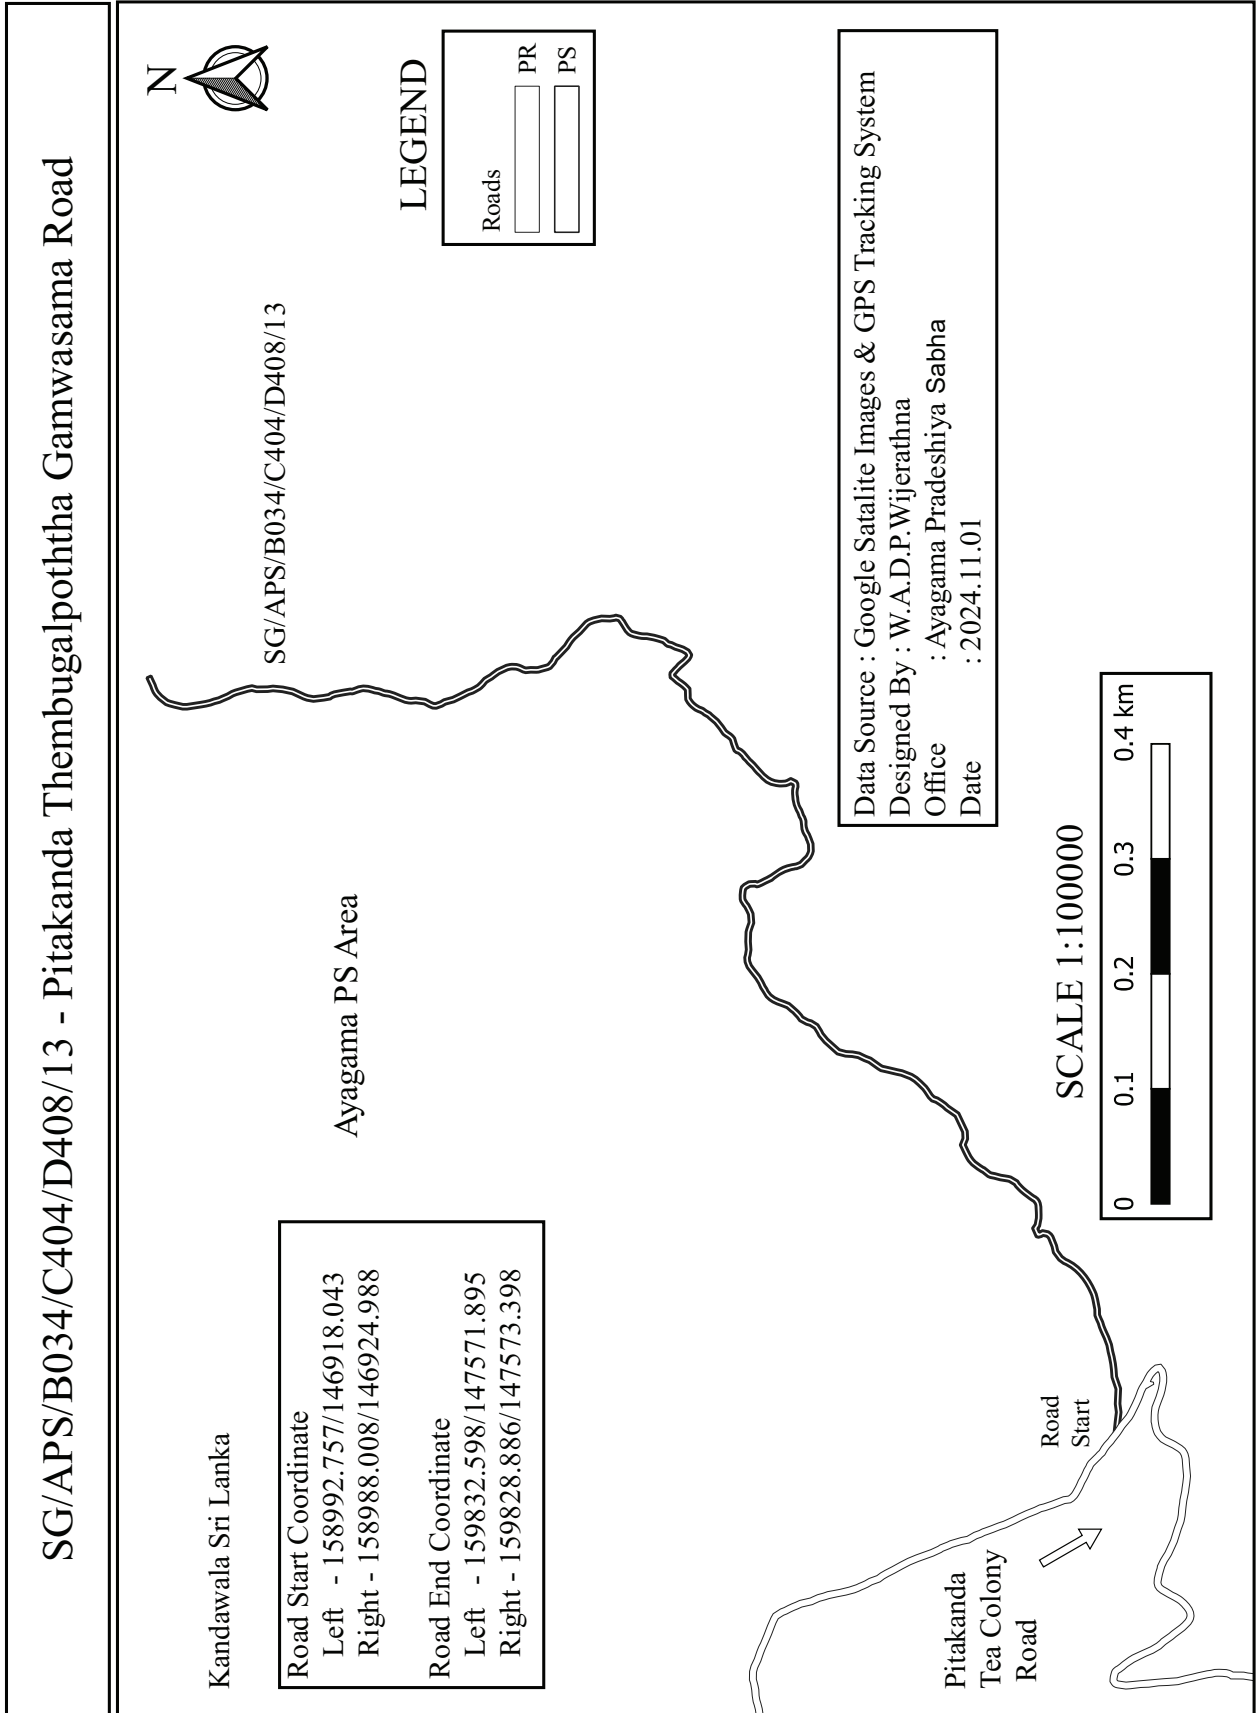


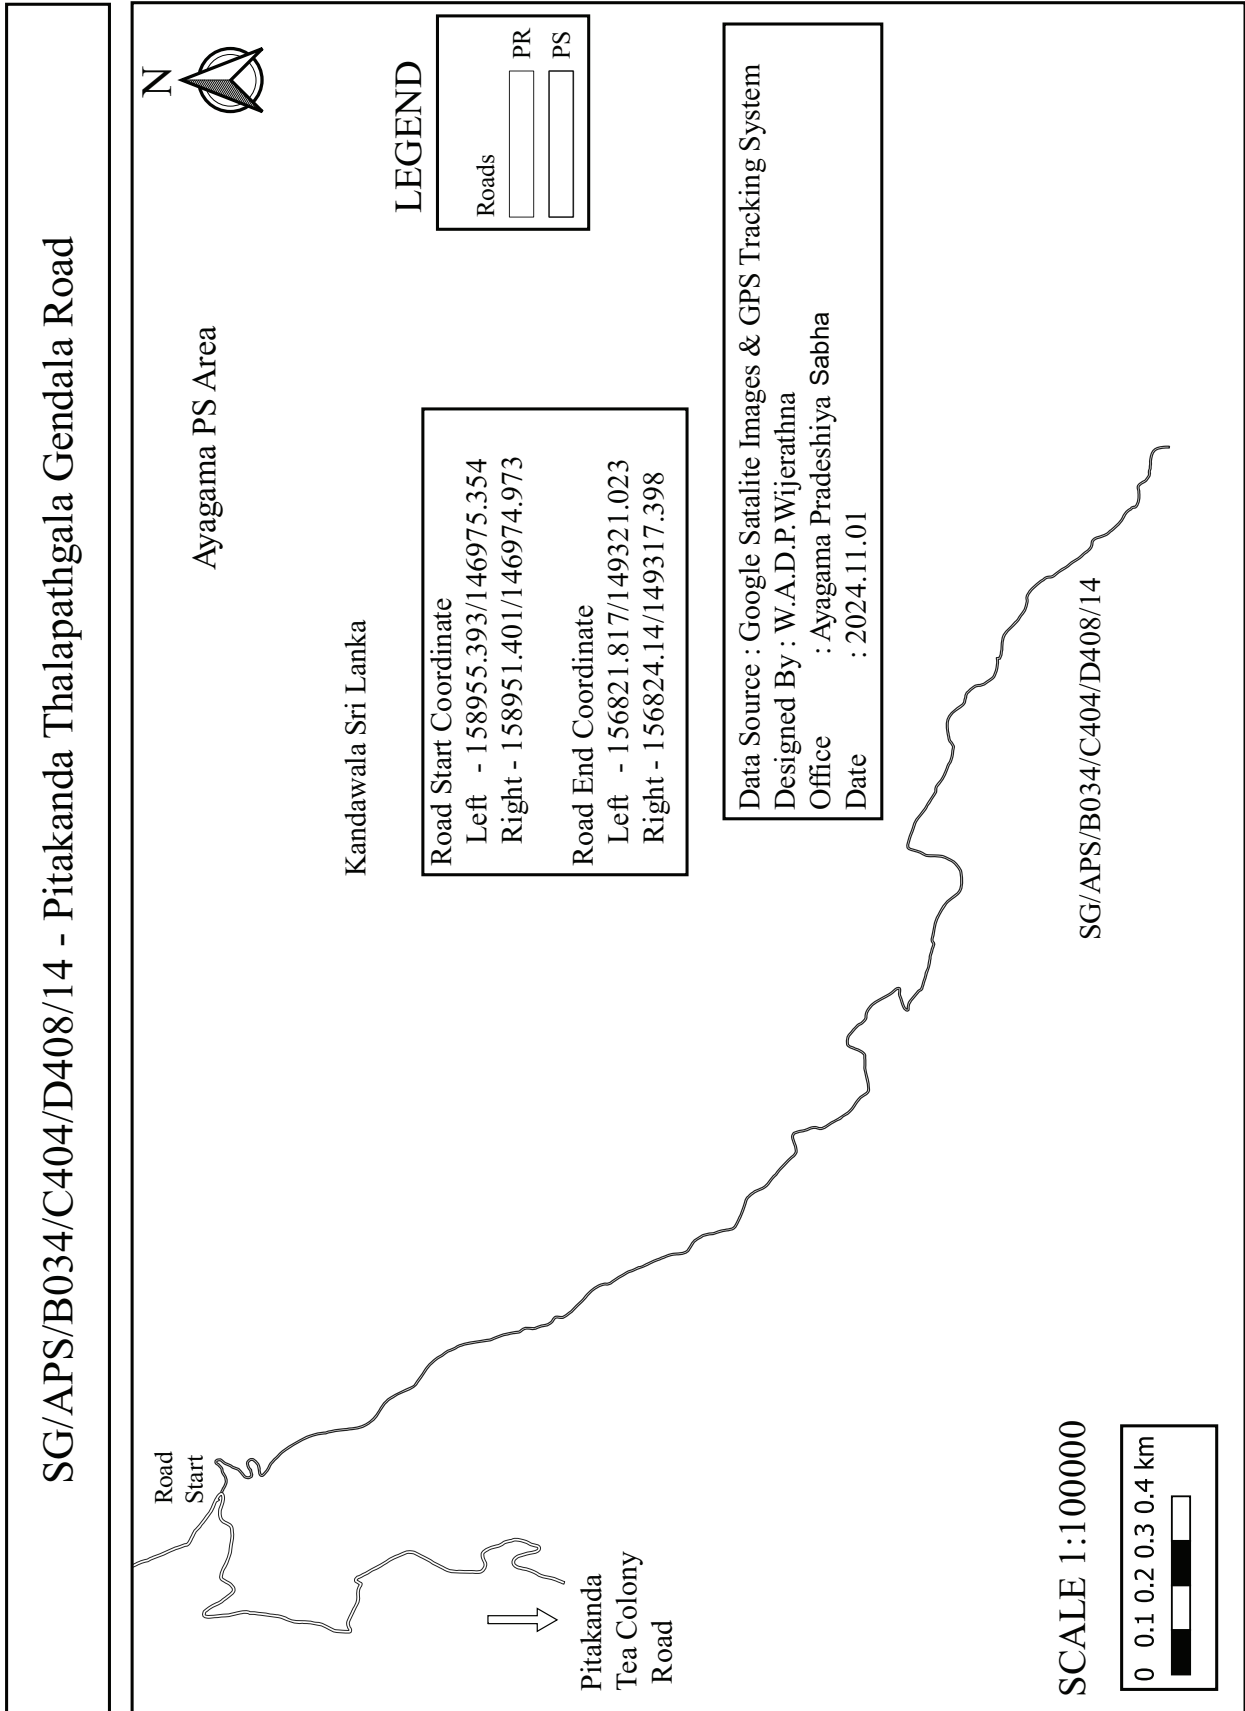

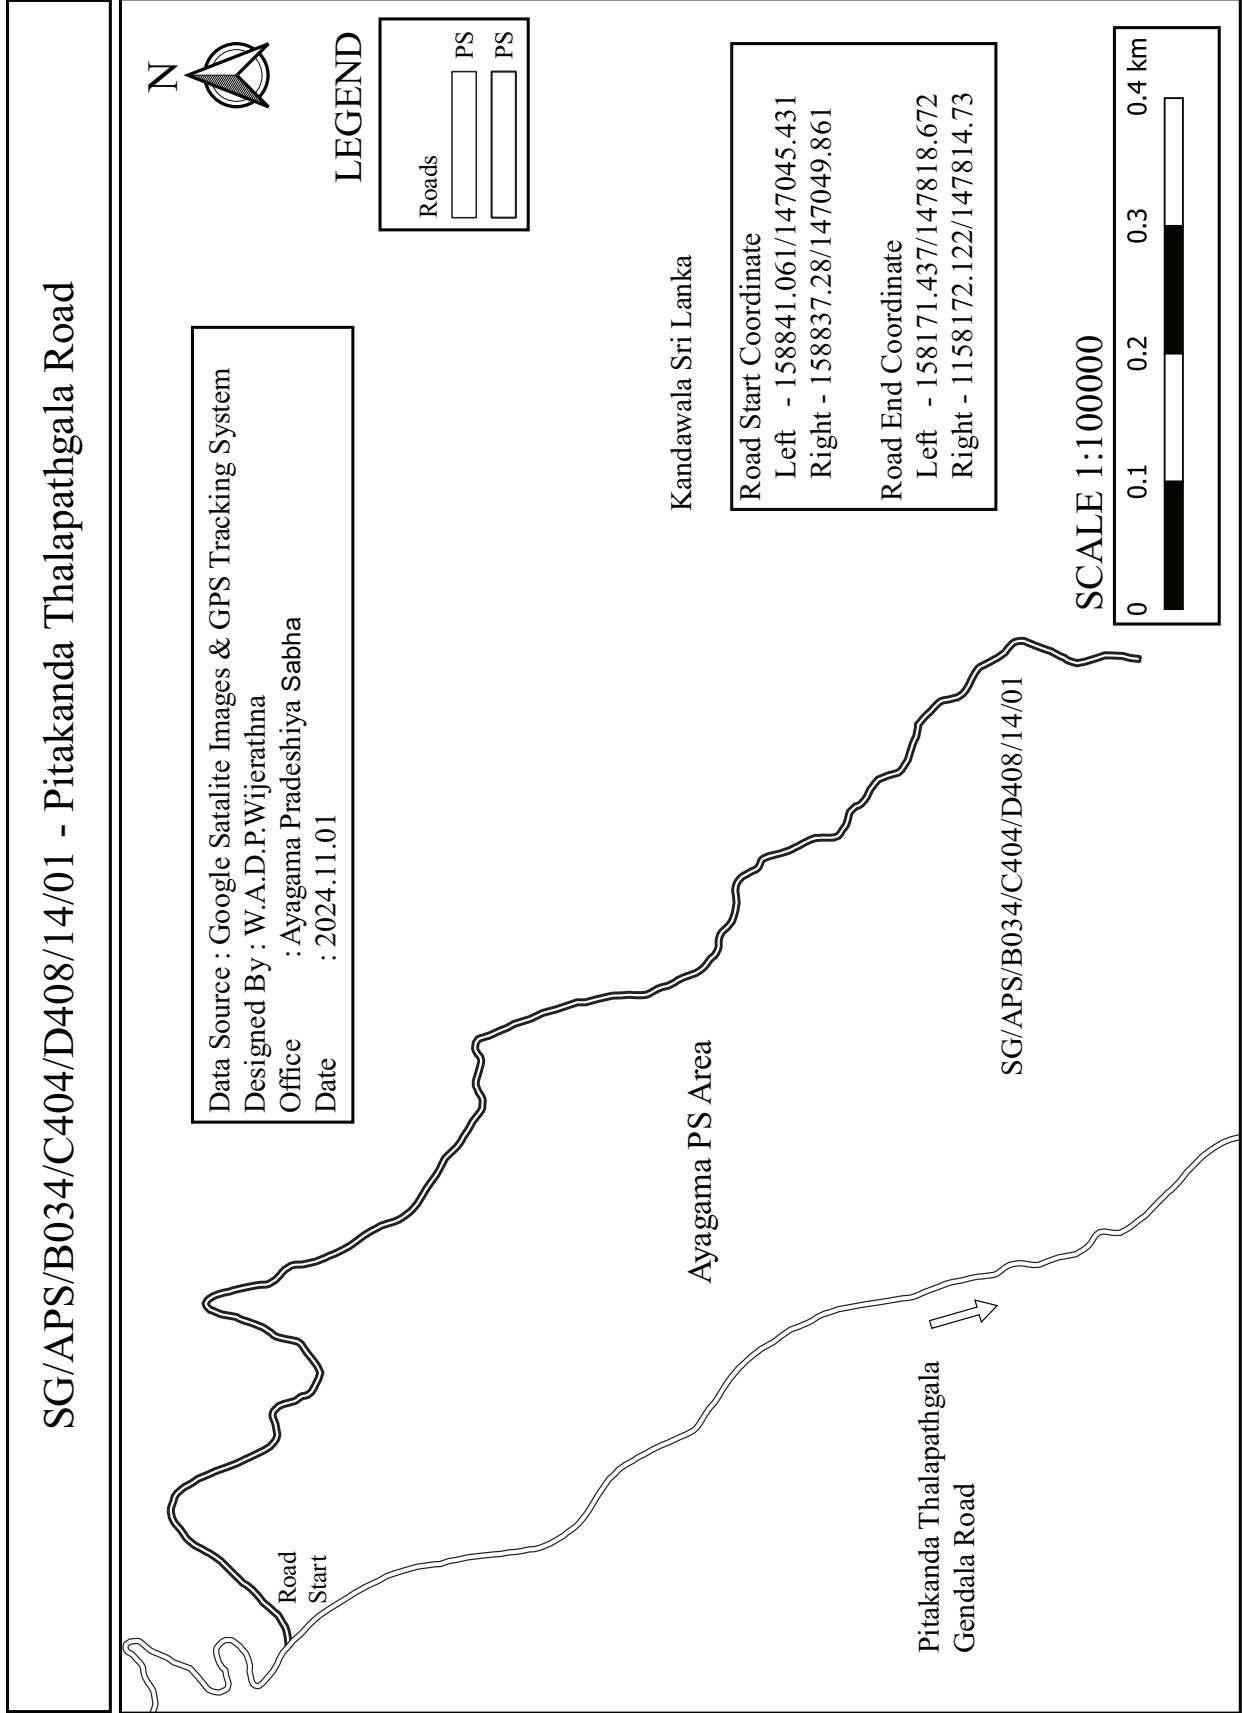



SG/APS/B034/C404/D408/14/02 - First Lane of Pitakanda Thalpathgala Road

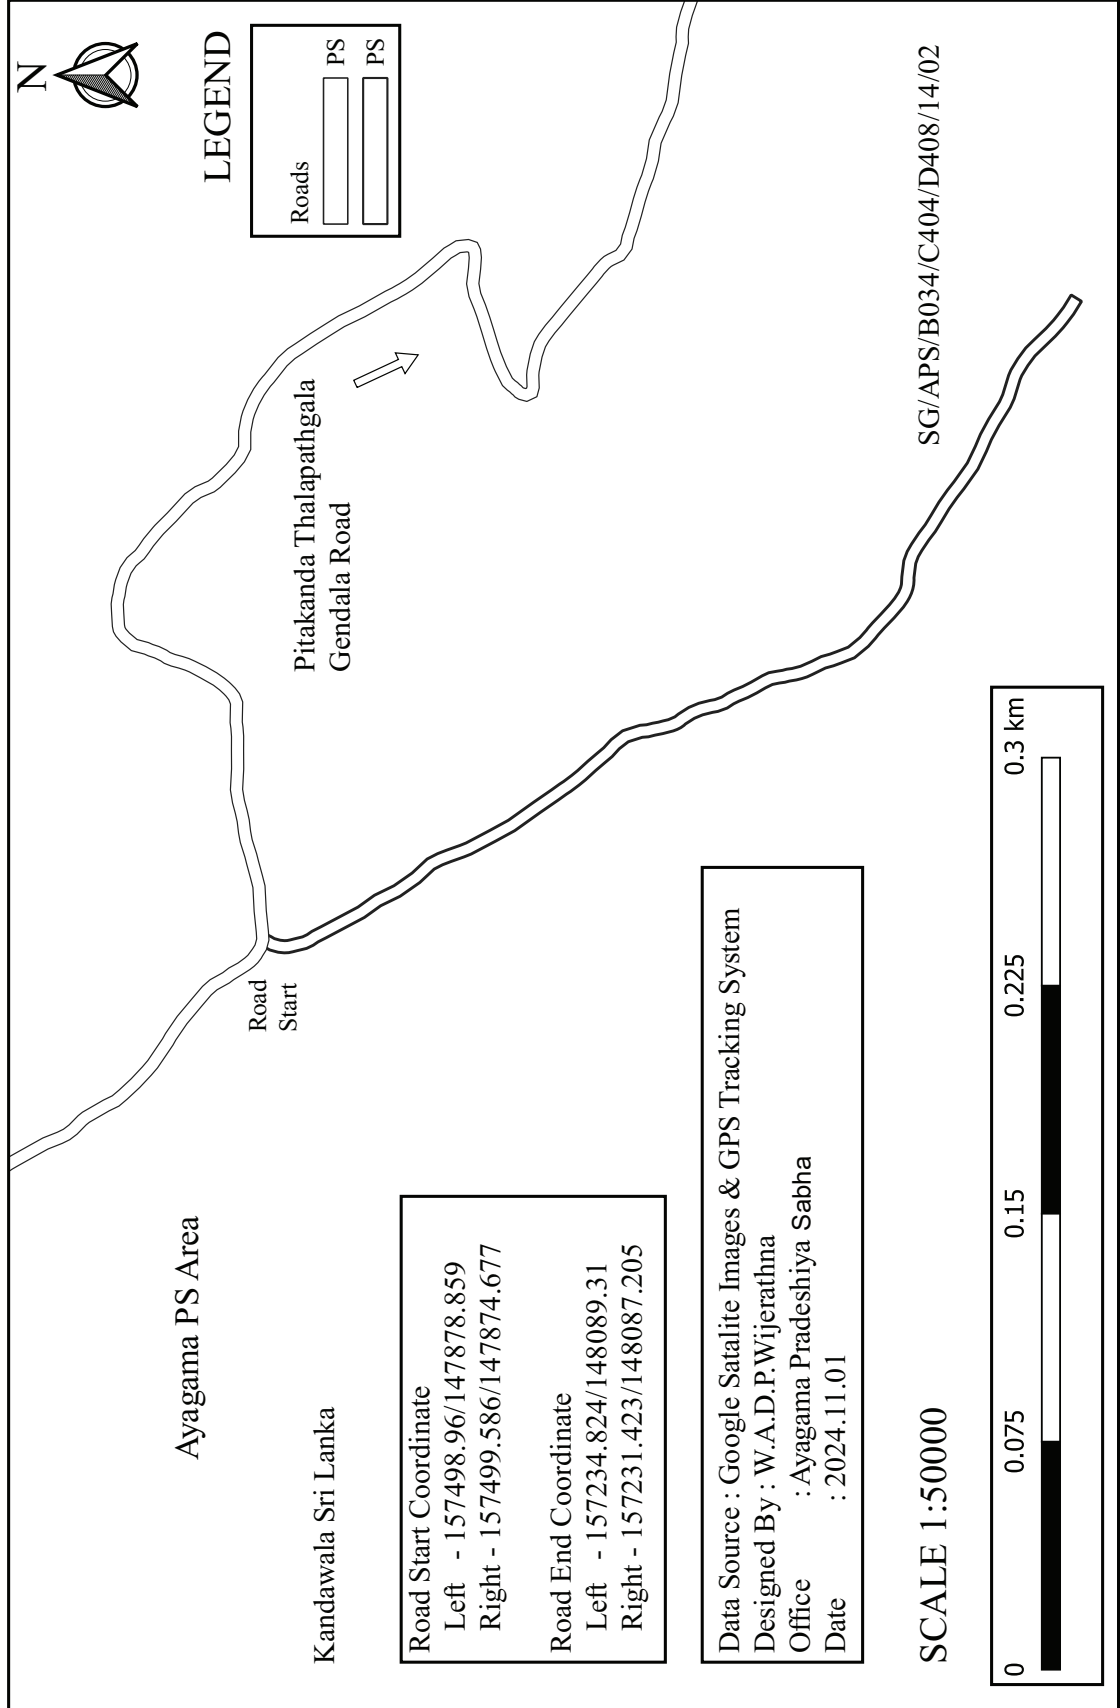


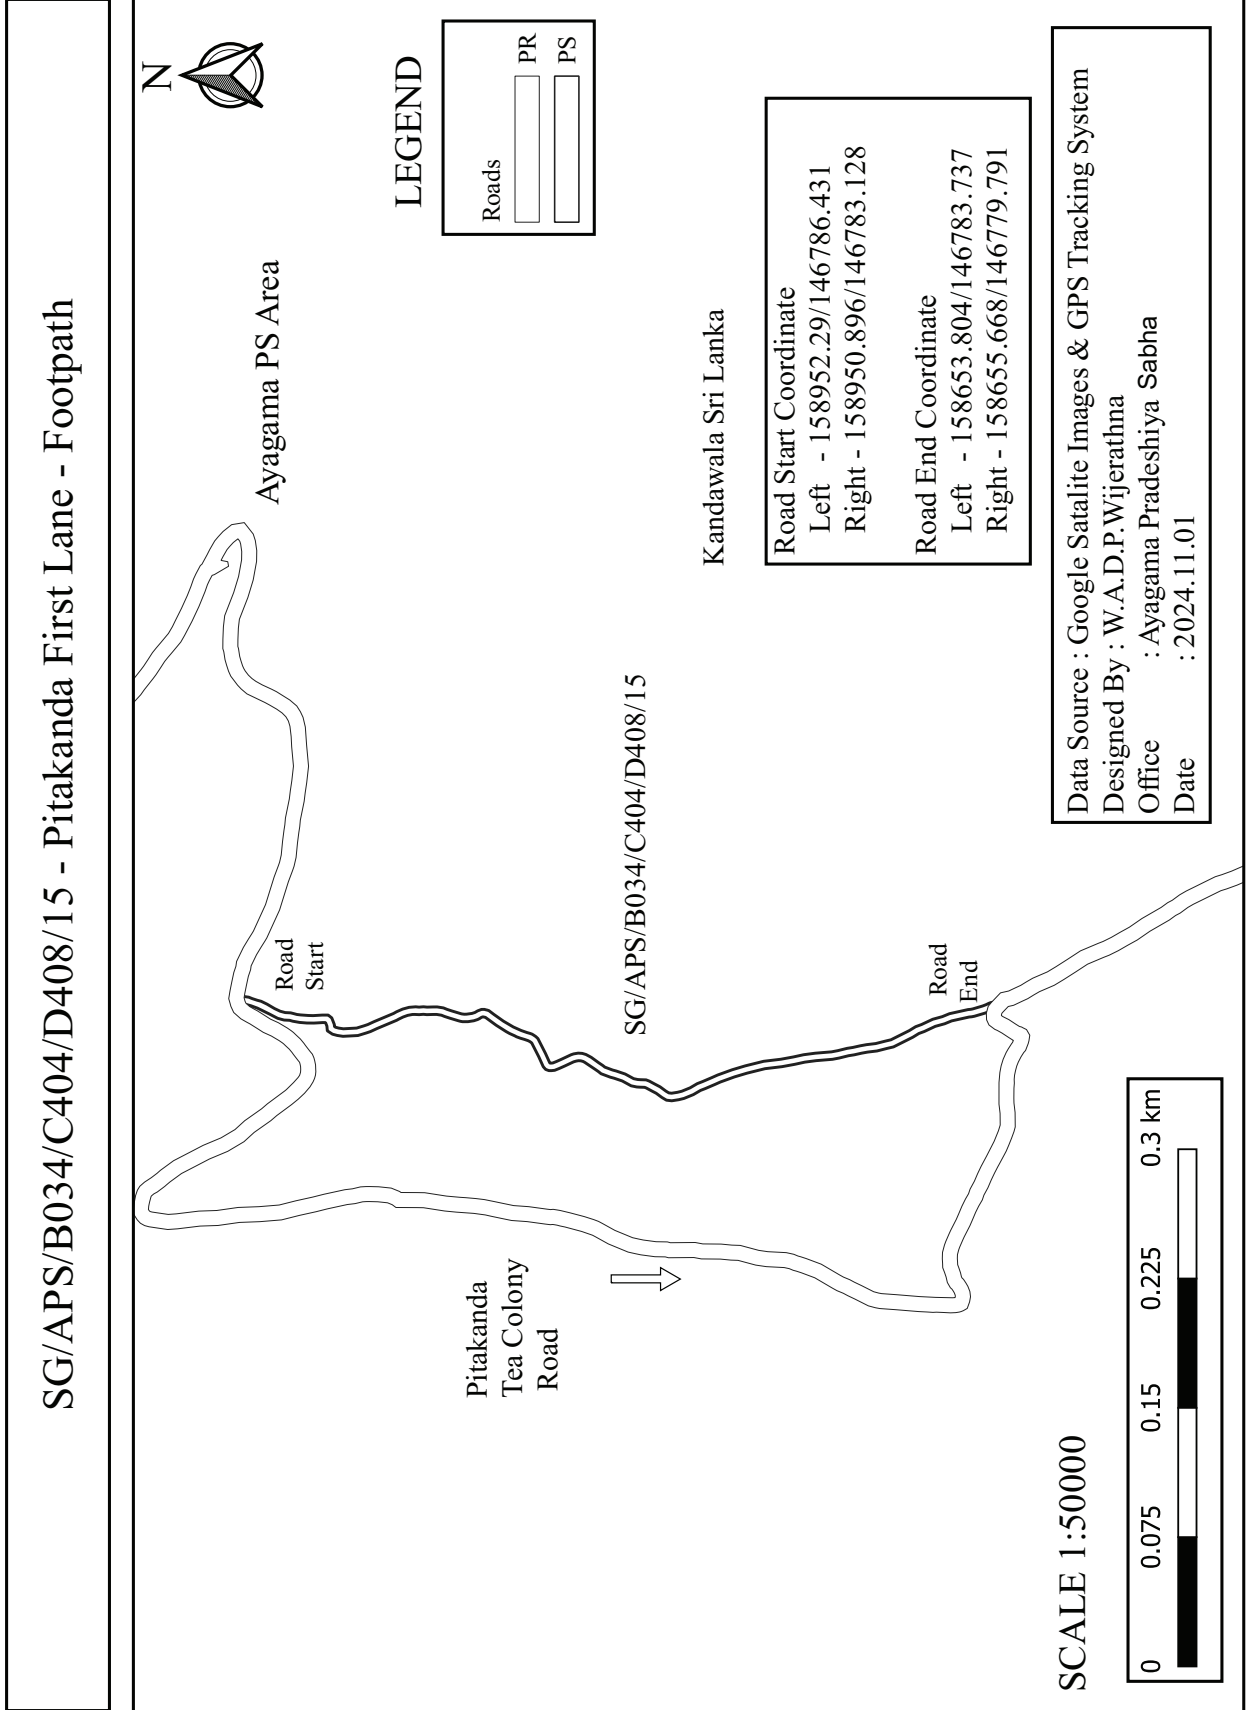



SG/APS/B034/C404/D408/16 - Pitakanda Panwilathenna Road

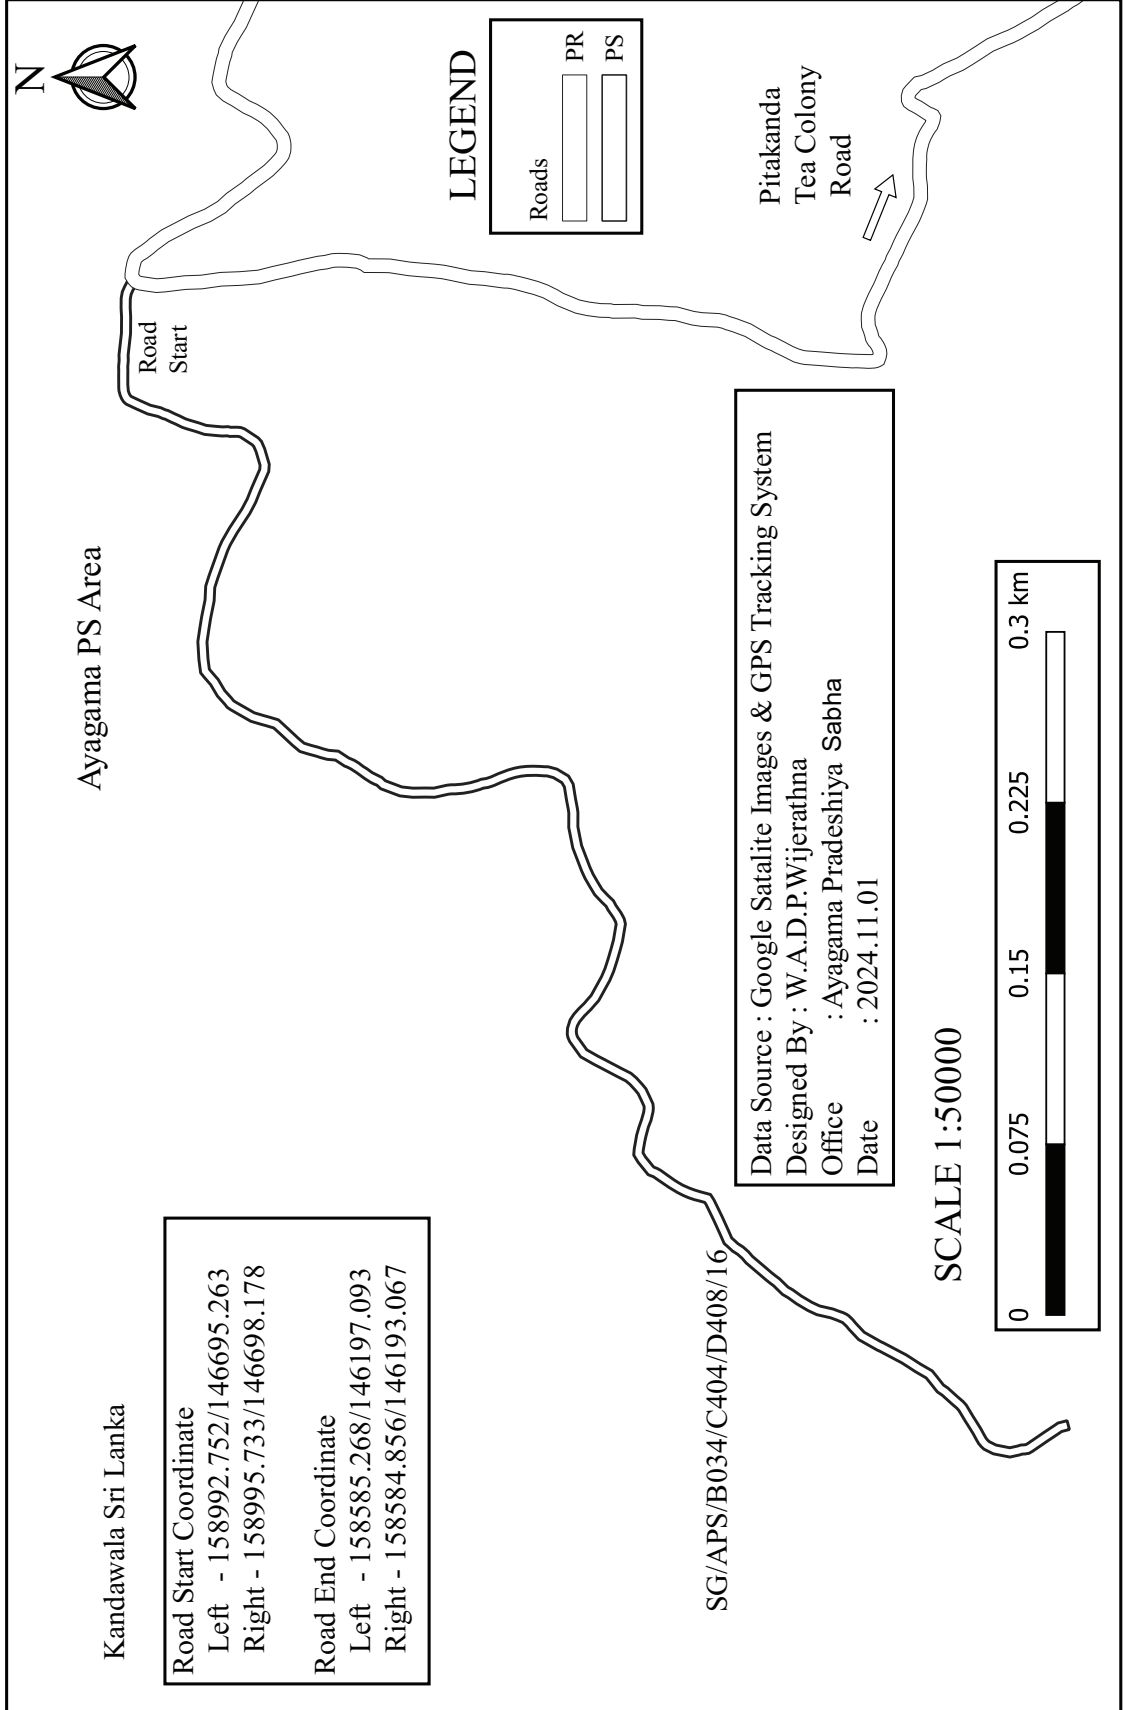

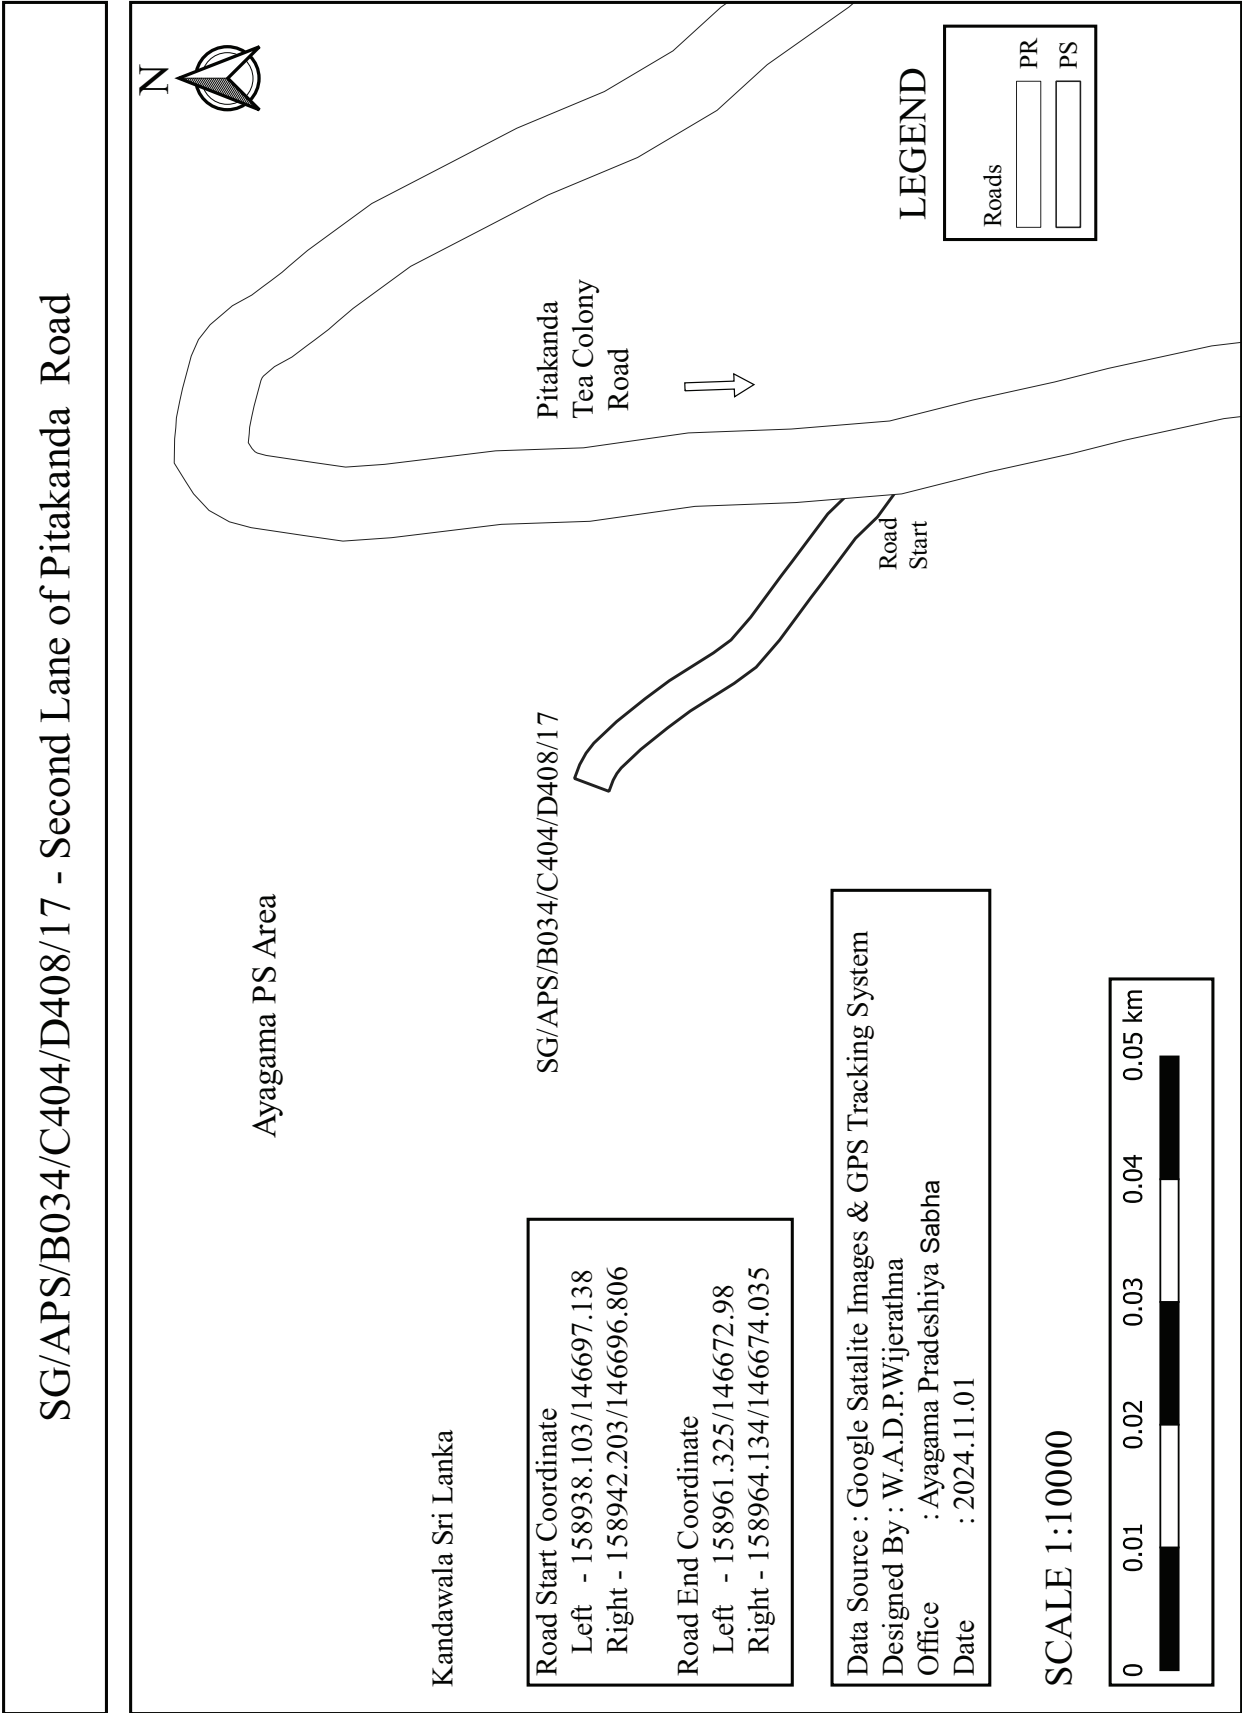


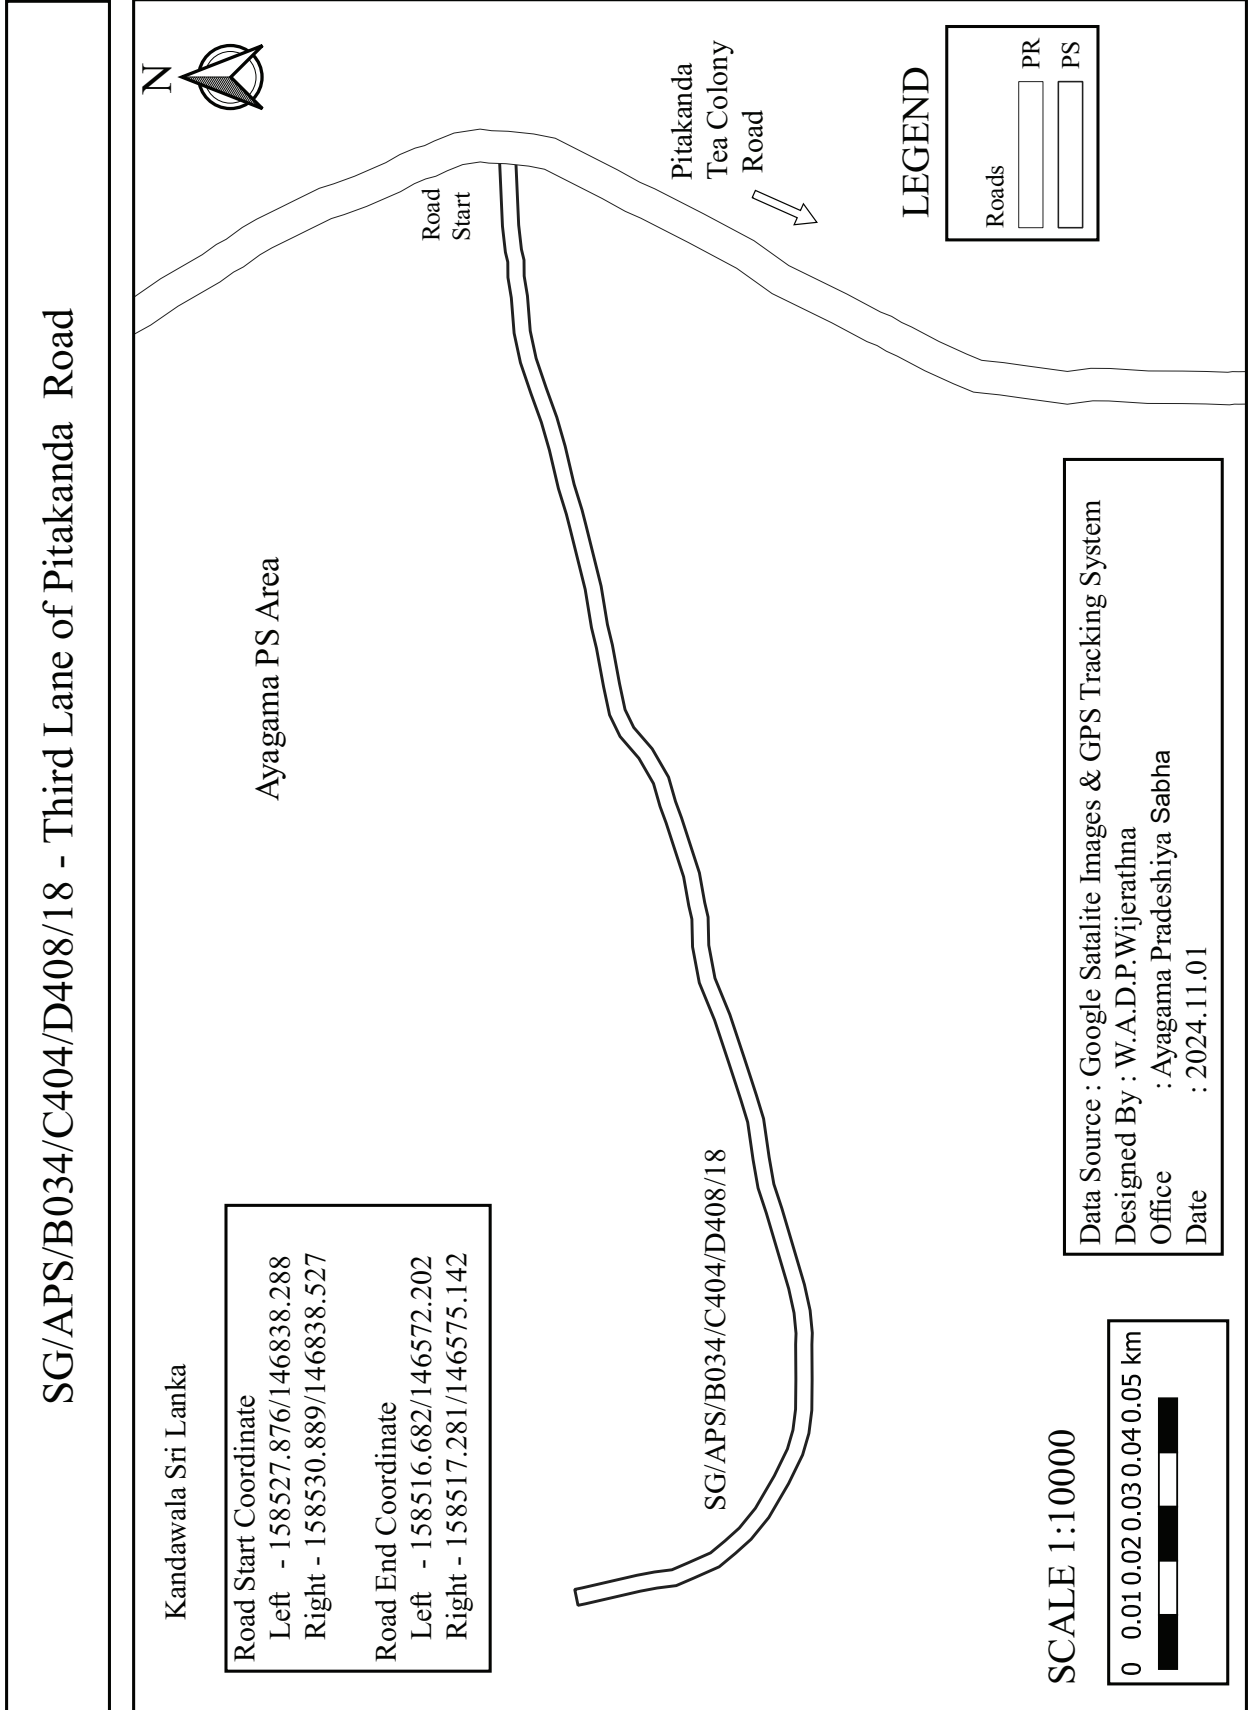

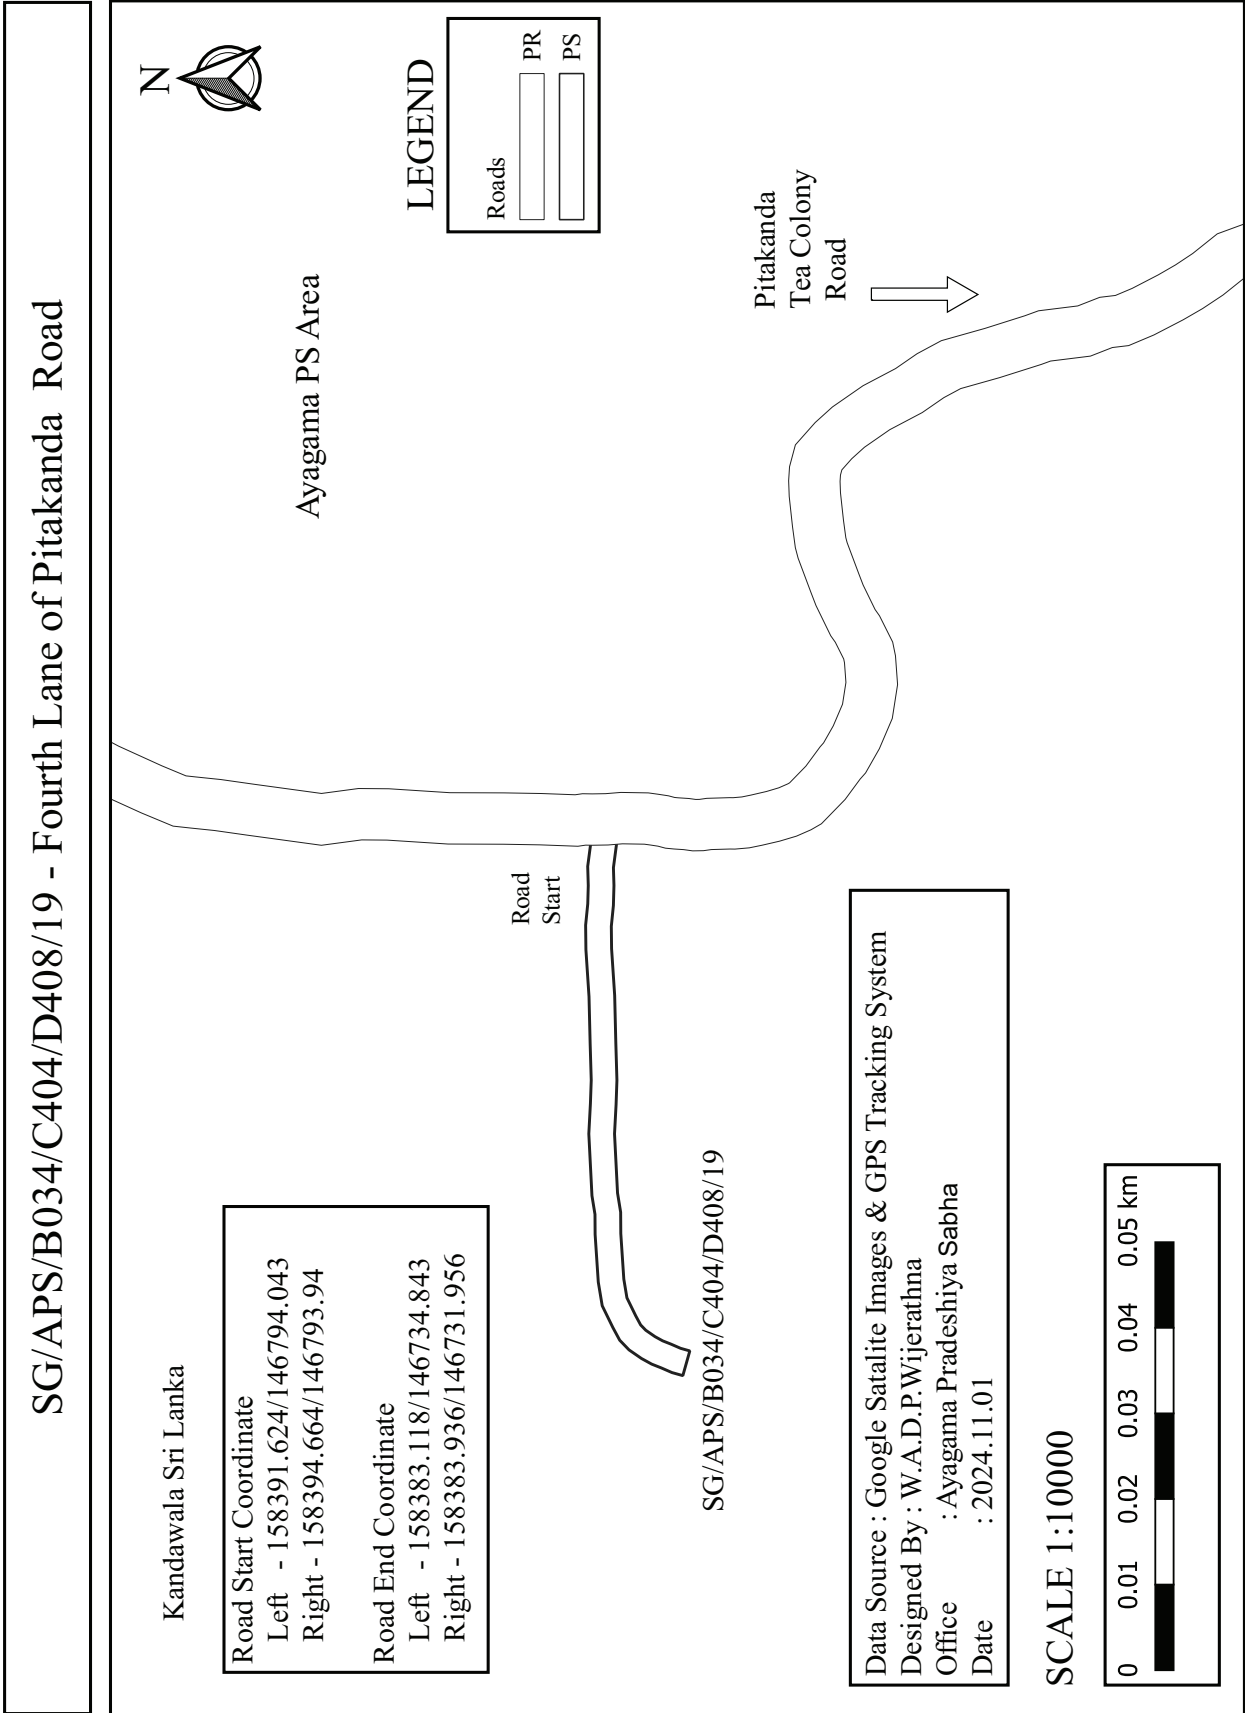


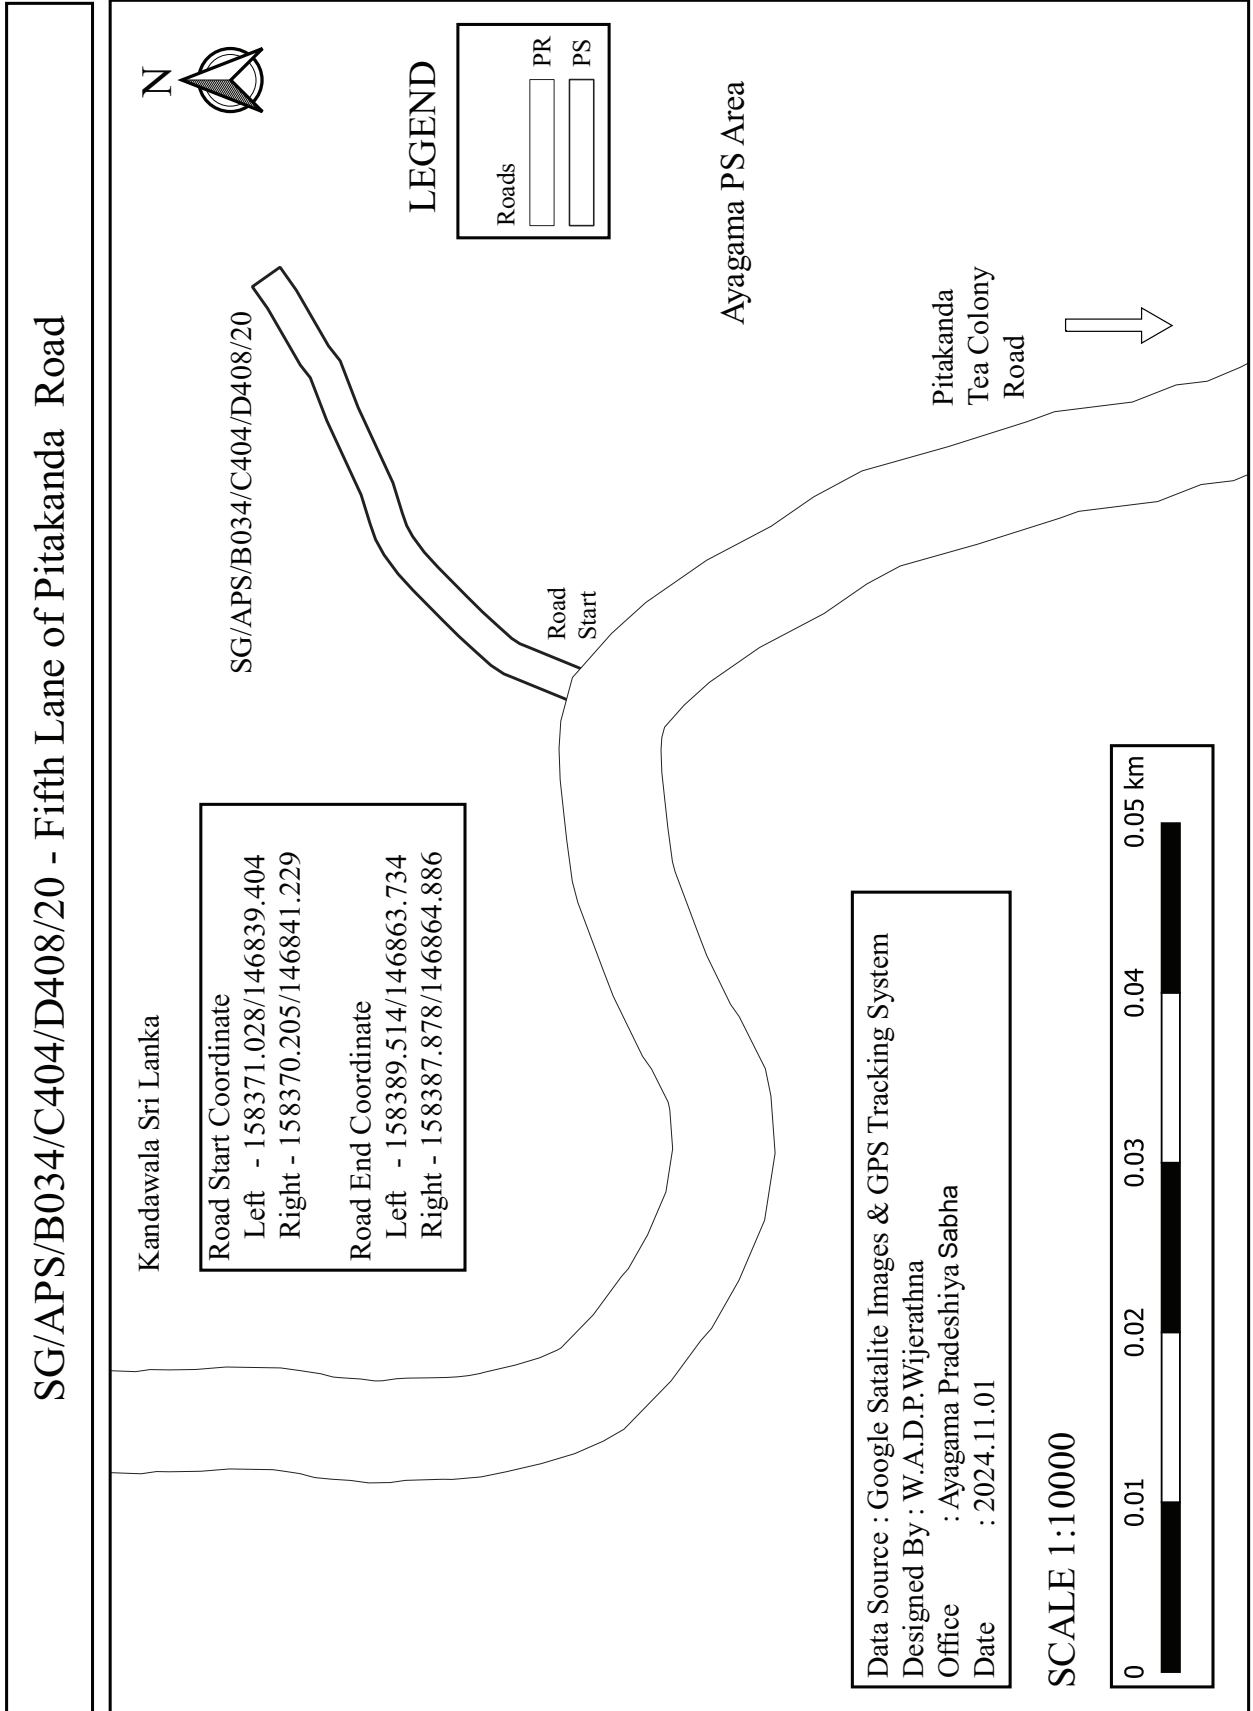


SG/APS/B034/C404/D408/21 - Sixth Lane of Pitakanda Road

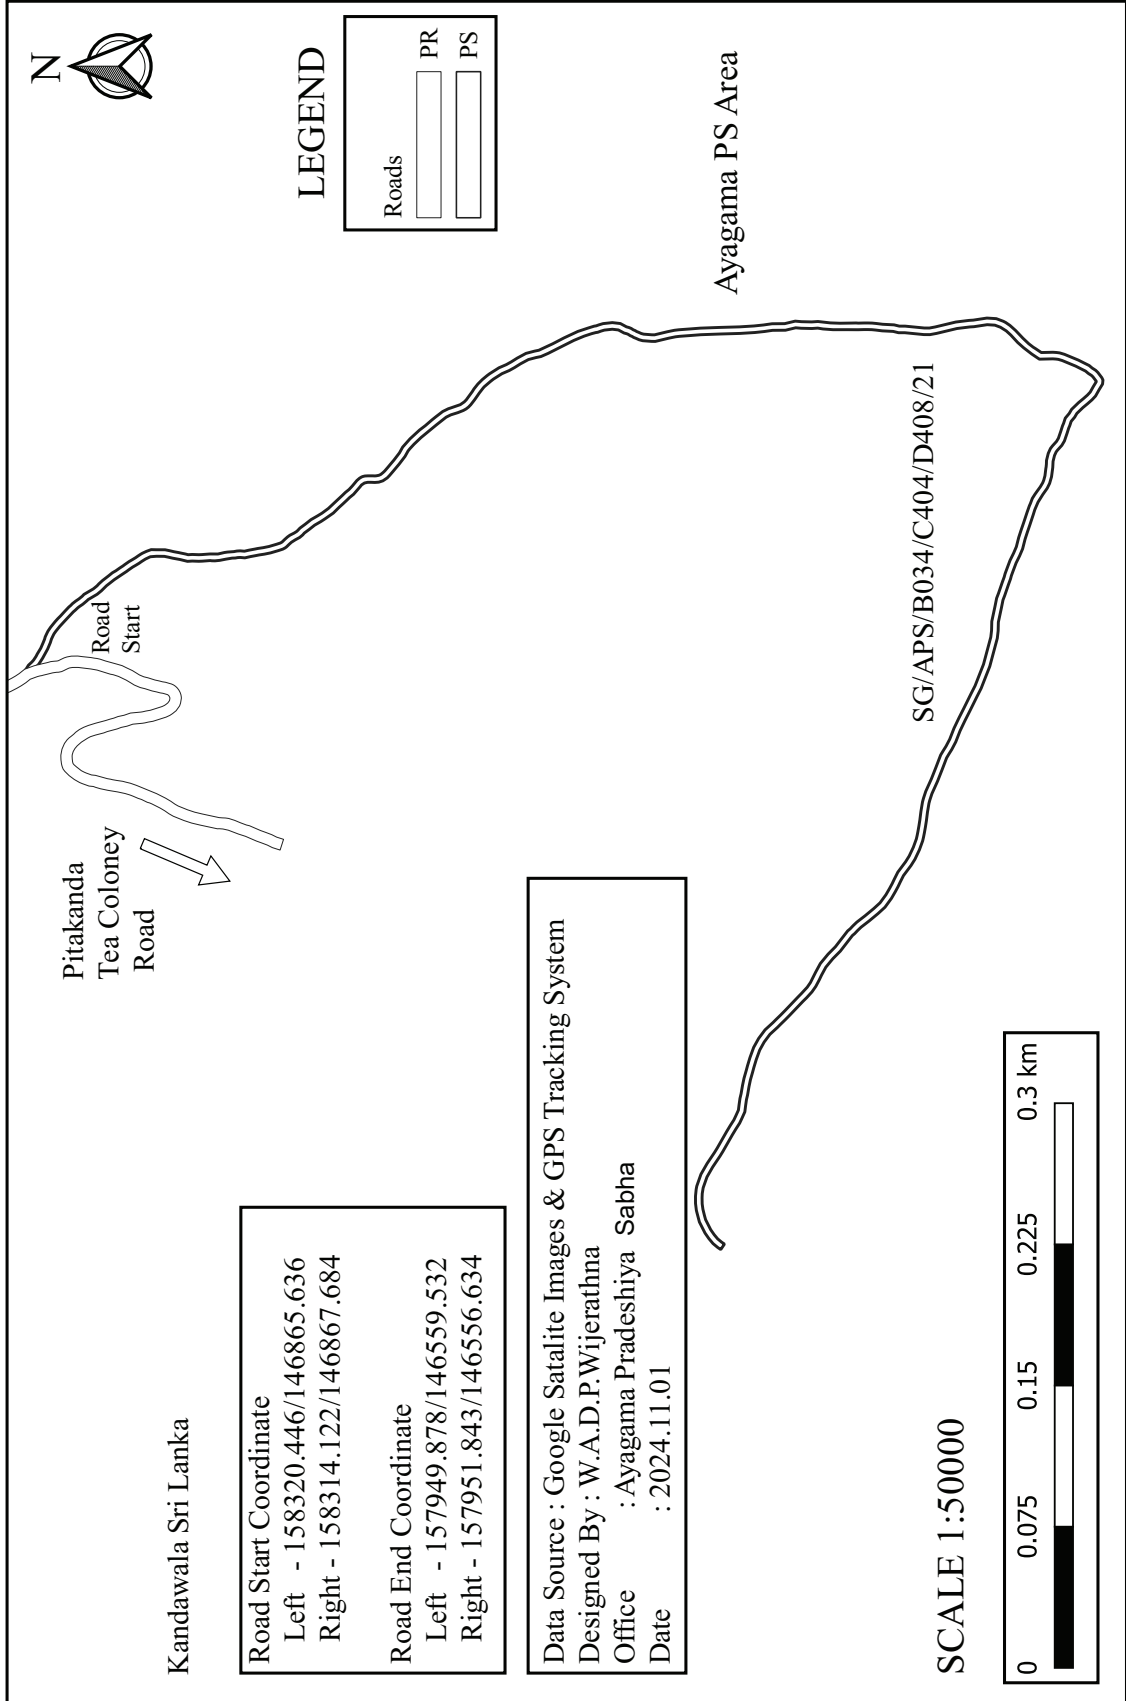


SG/APS/B034/C404/D408/21/01 - First By Pass - Footpath of Sixth Lane of Pitakanda Road

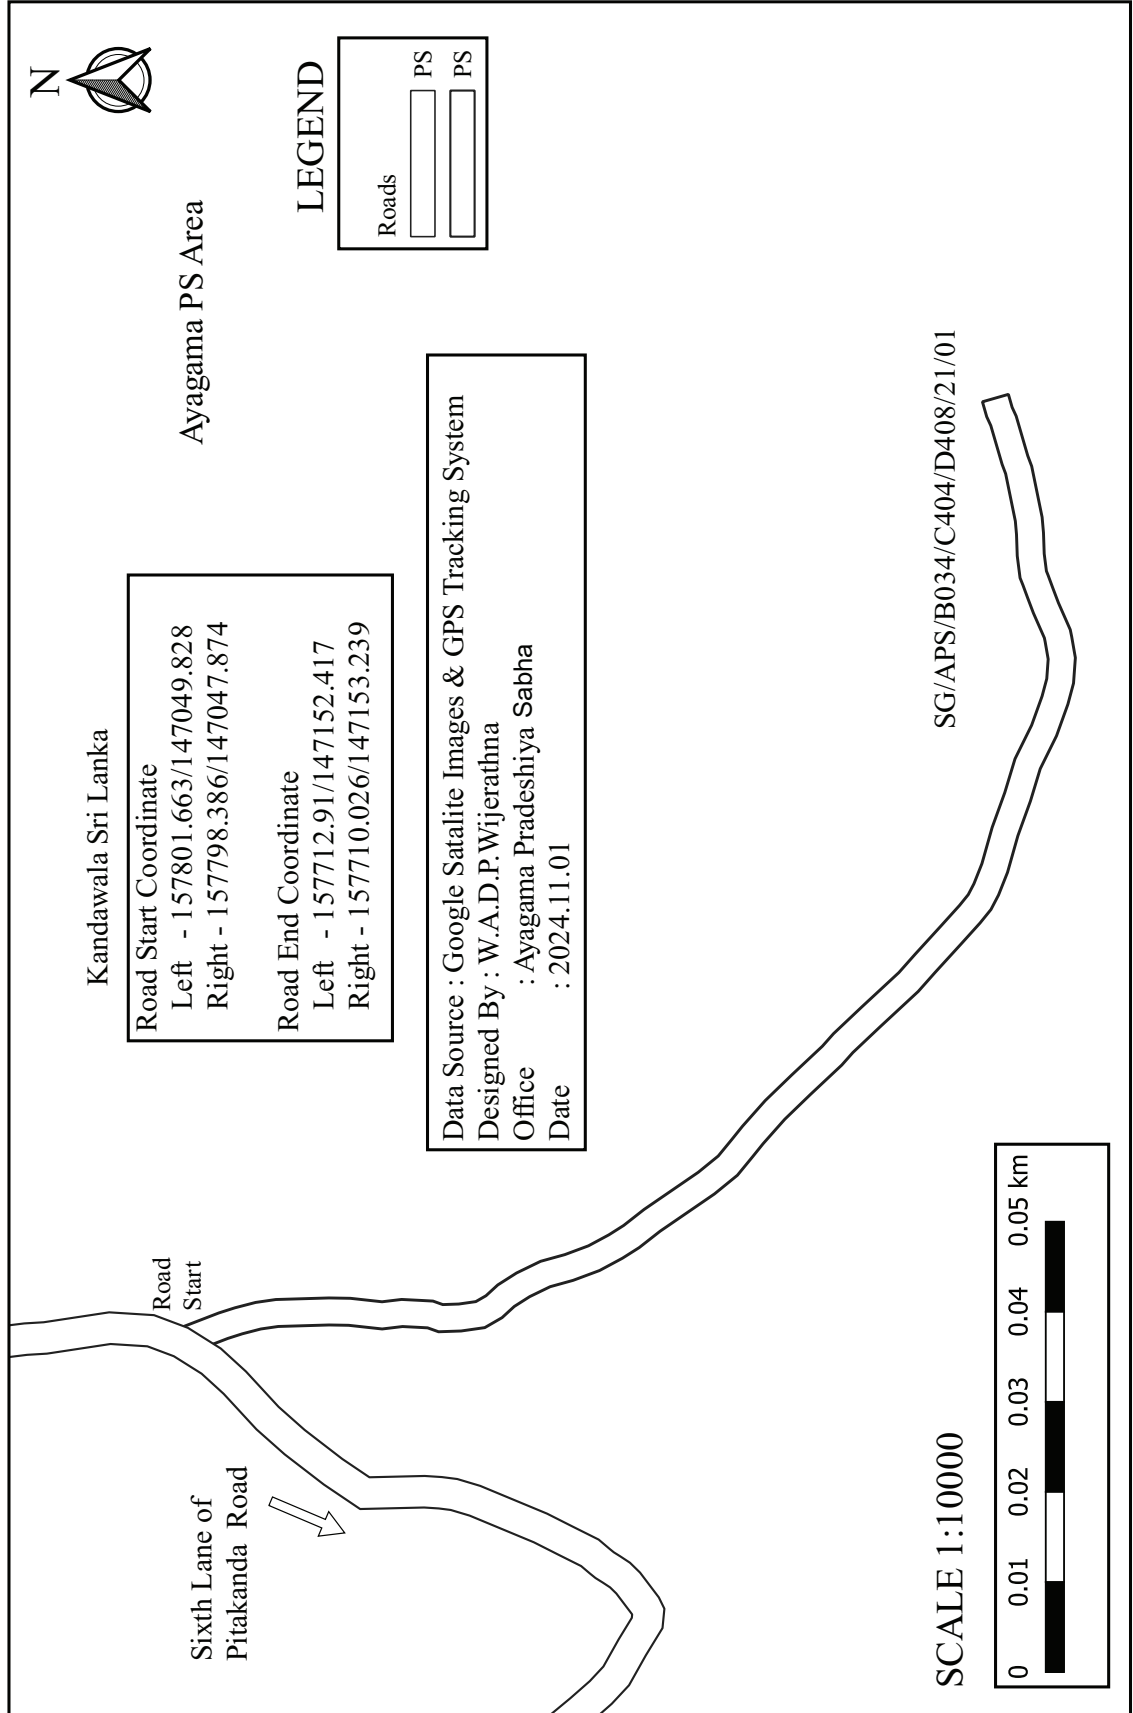

SG/APS/B034/C404/D408/22 - Pitakanda Gamsabha Foot Path

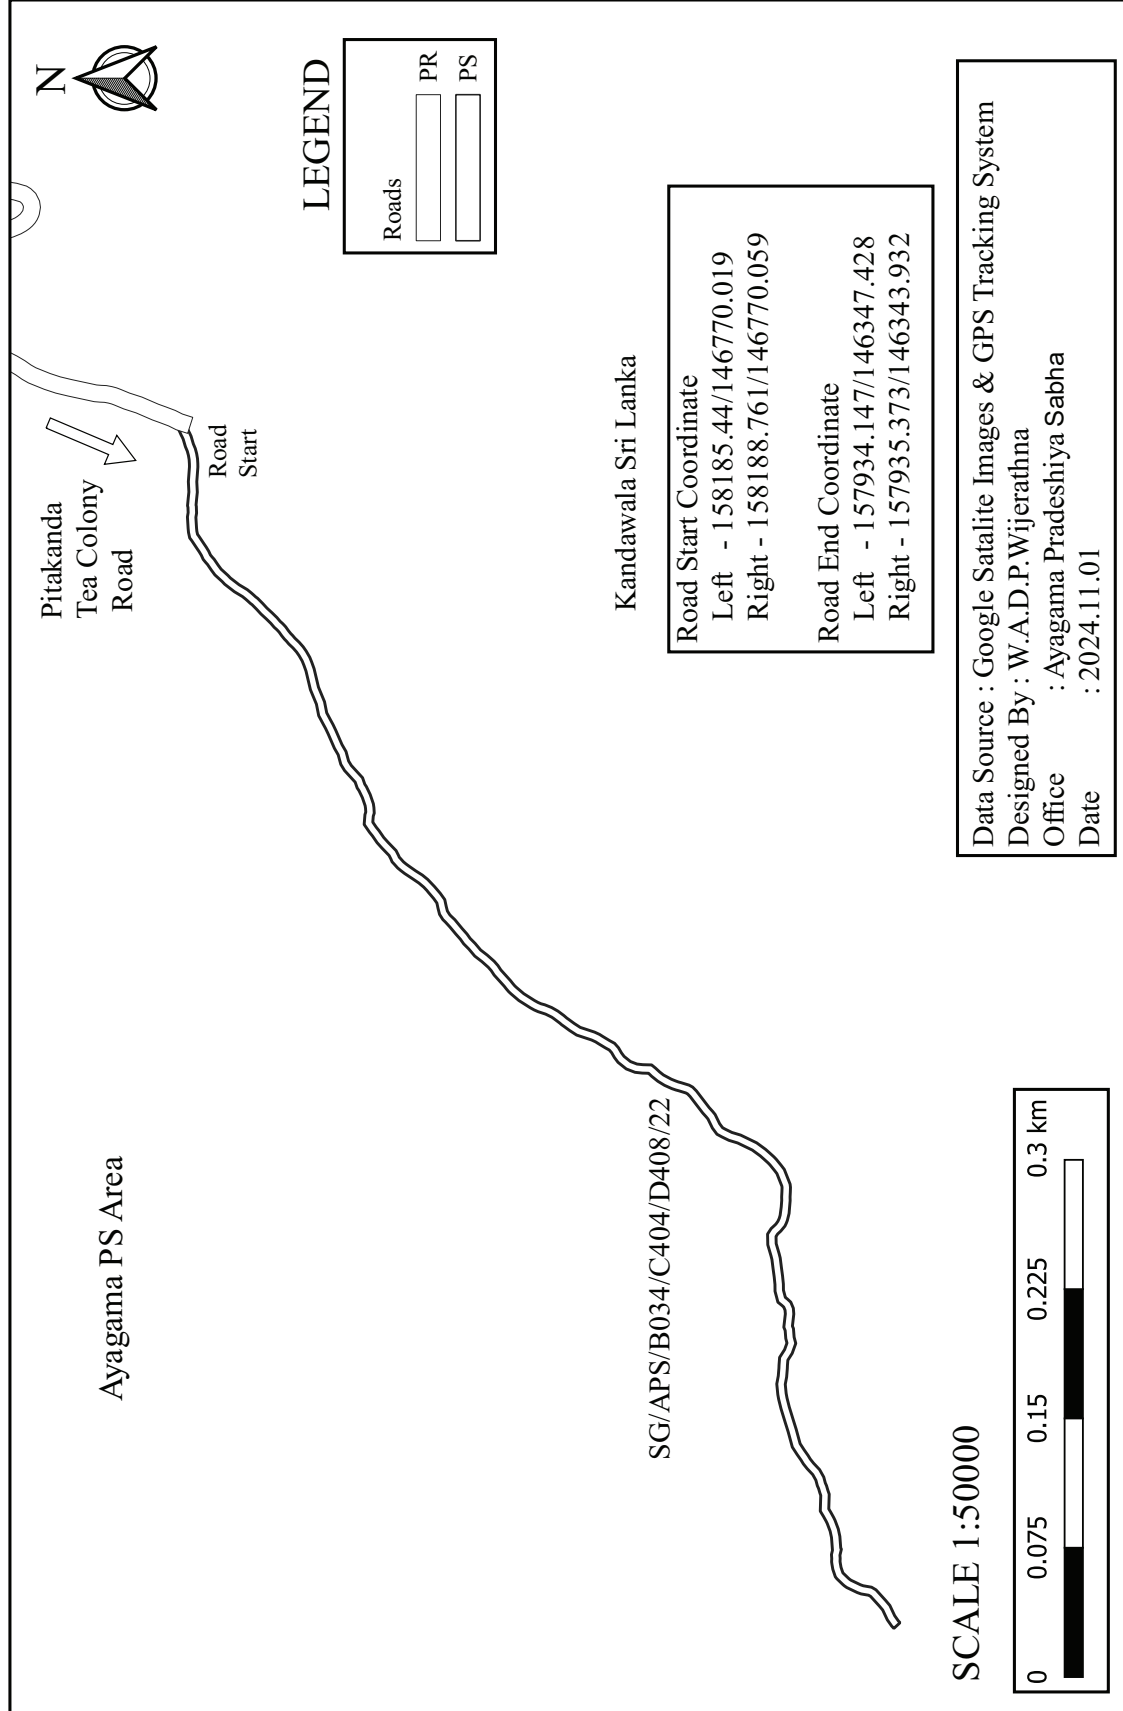

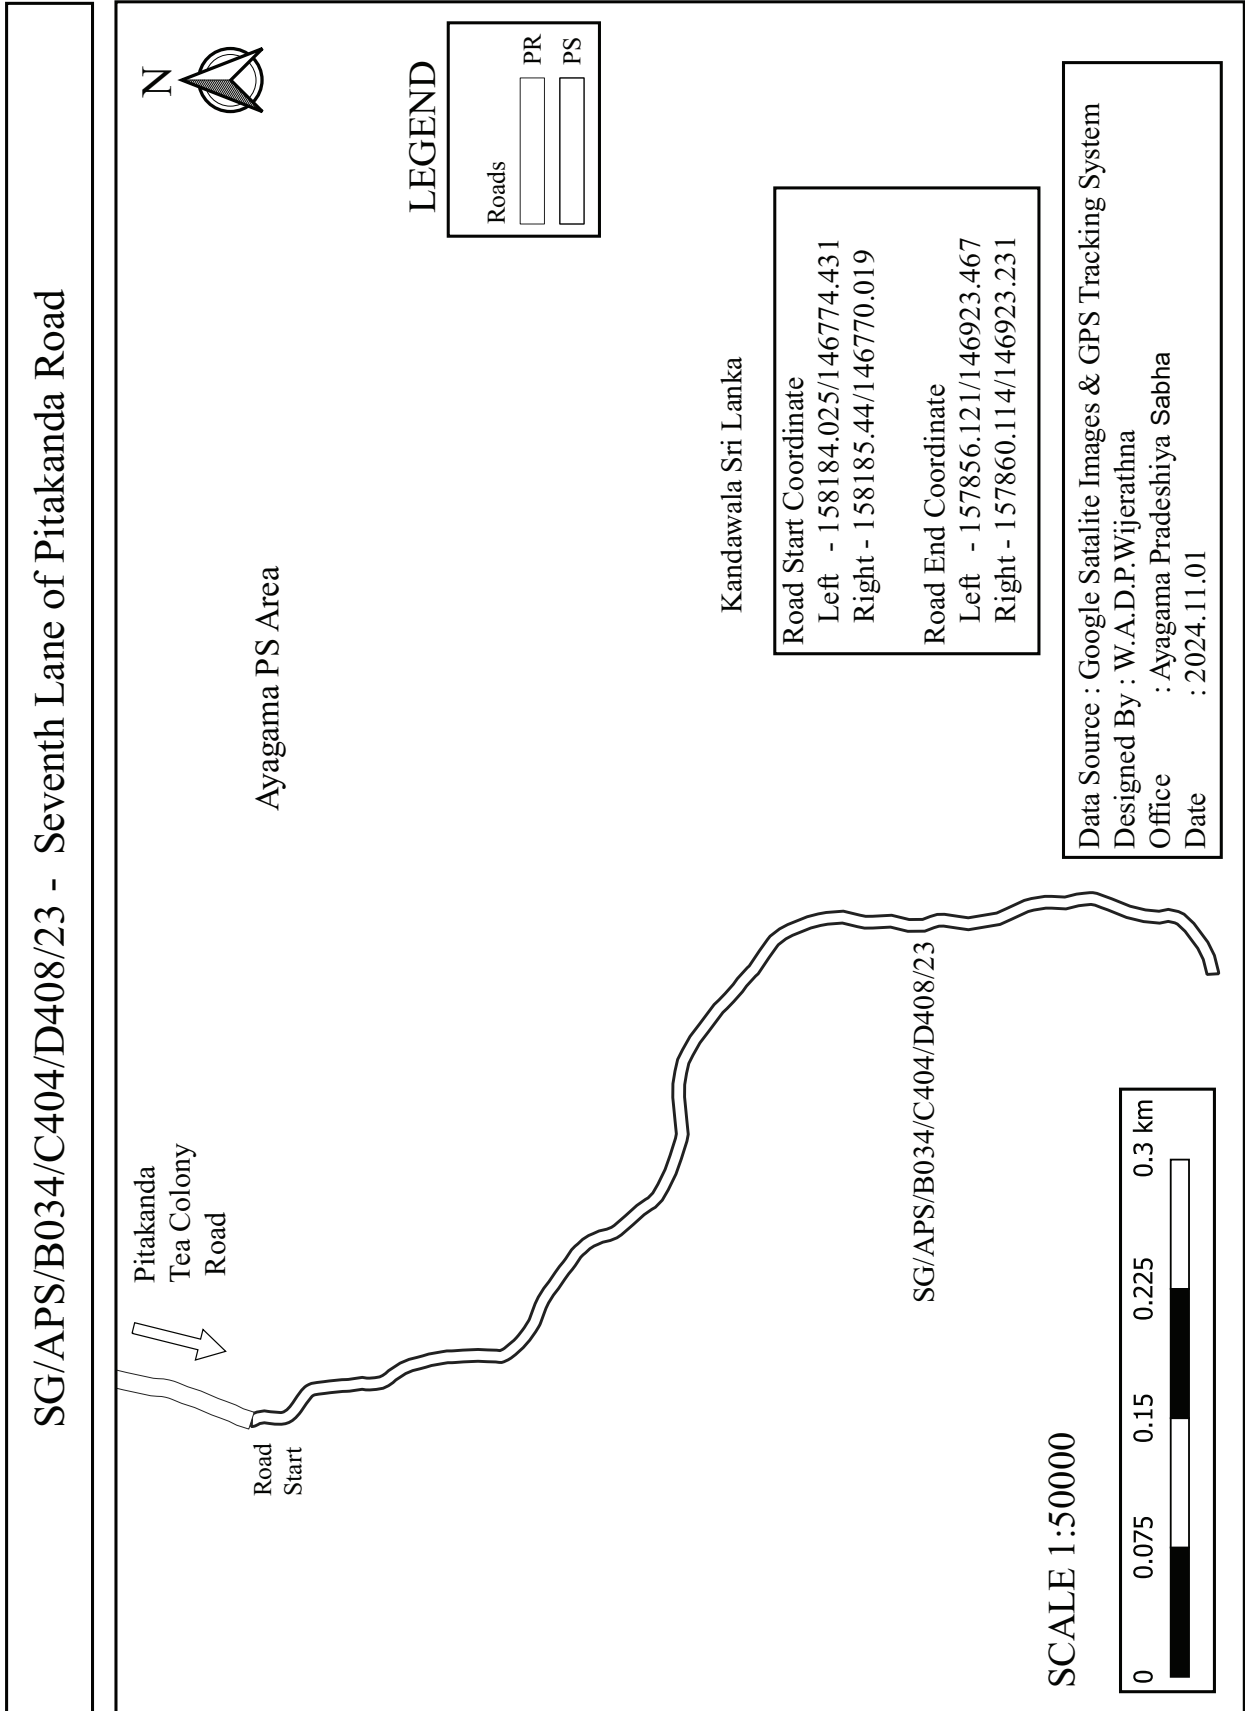

SG/APS/B034/C404/D406/01 - Ambagaha Junction Kalumediriya Road

Data Source : Google Satalite Images & GPS Tracking System

Designed By : W.A.D.P.Wijerathna

Office : Ayagama Pradeshiya Sabha

Date : 2024.11.01



Ayagama PS Area

Kandawala Sri Lanka

SG/APS/B034/C404/D406/01

LEGEND

Road Start Coordinate
 Left - 161131.443/145171.071
 Right - 161134.896/145173.252

Road End Coordinate
 Left - 162750.019/144418.317
 Right - 162752.289/144421.611


Roads	PR	PR	PS


Tea Colony Heressa Road


Road
Start


Ayagama Gawaragiriya Road


SCALE 1:250000

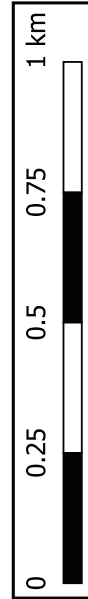


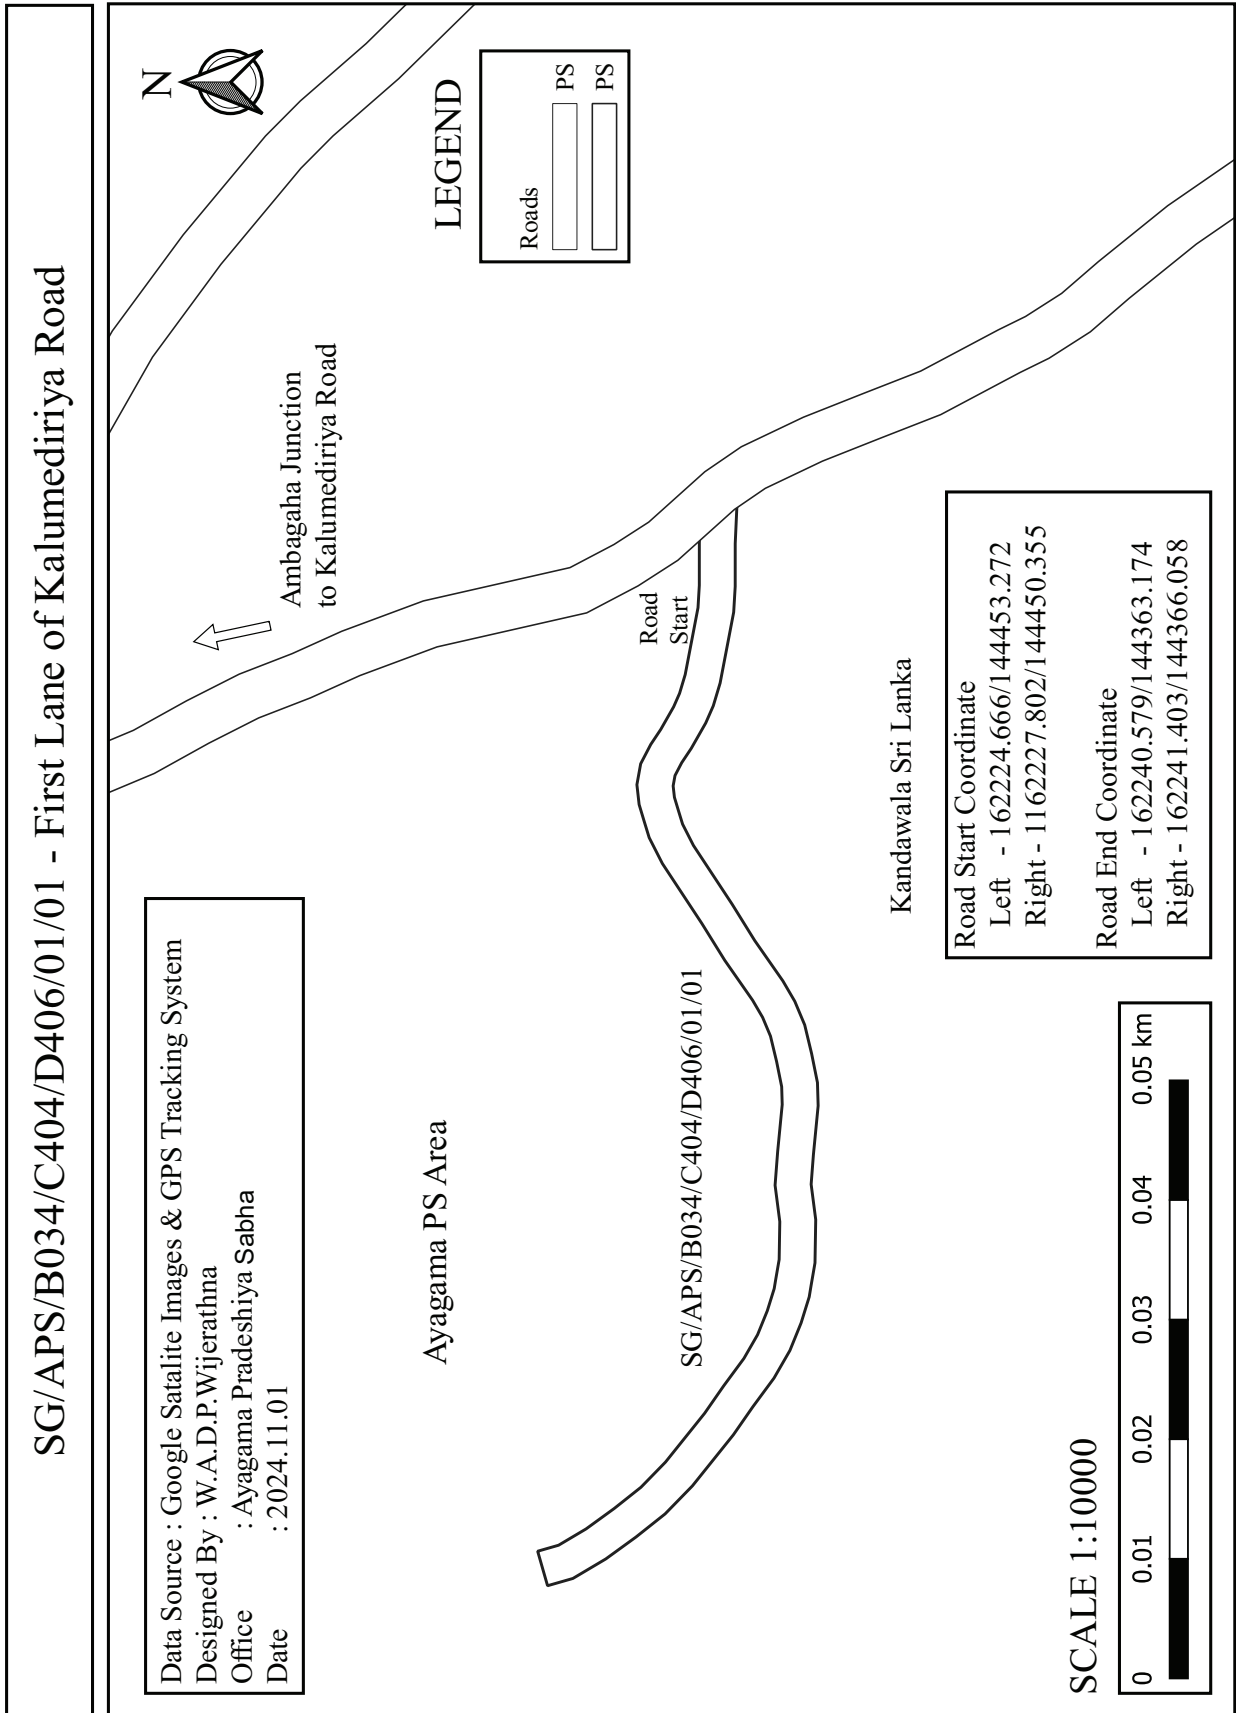


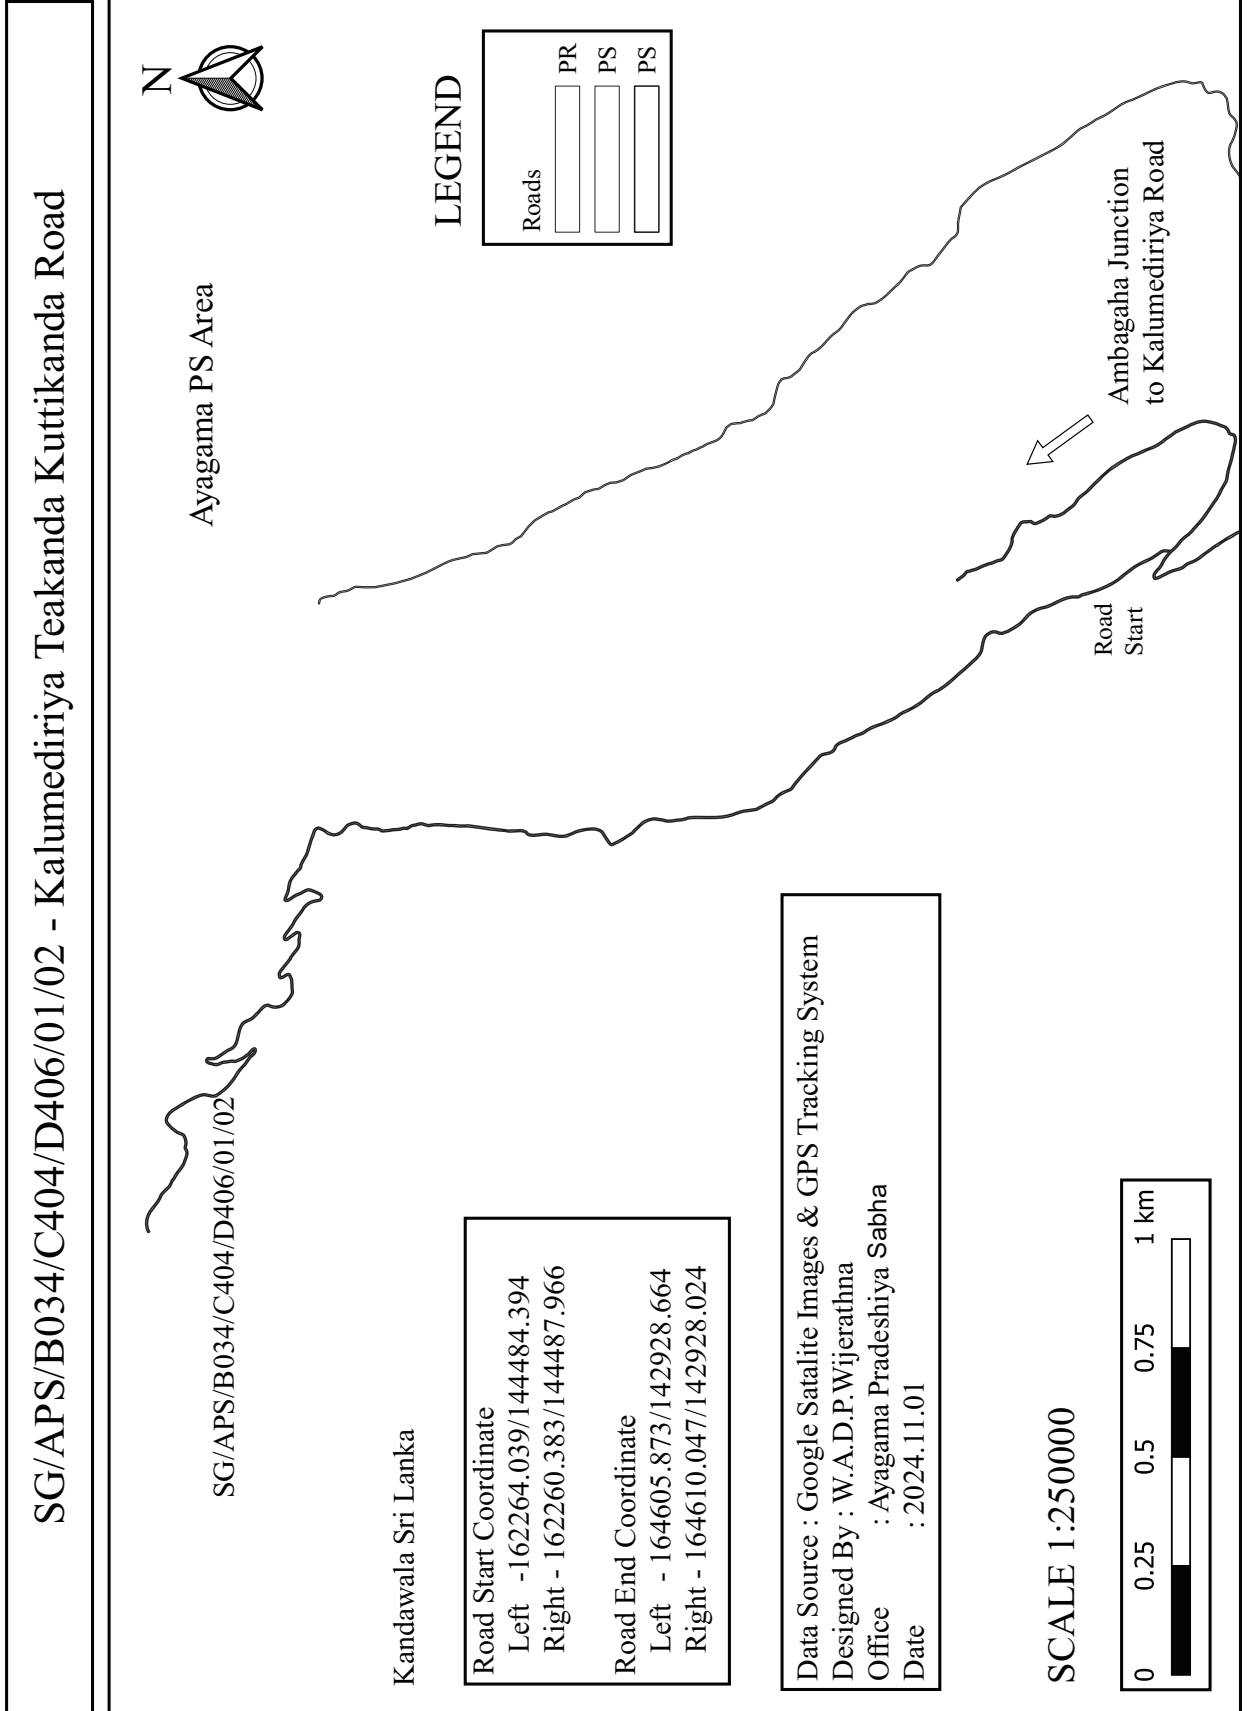


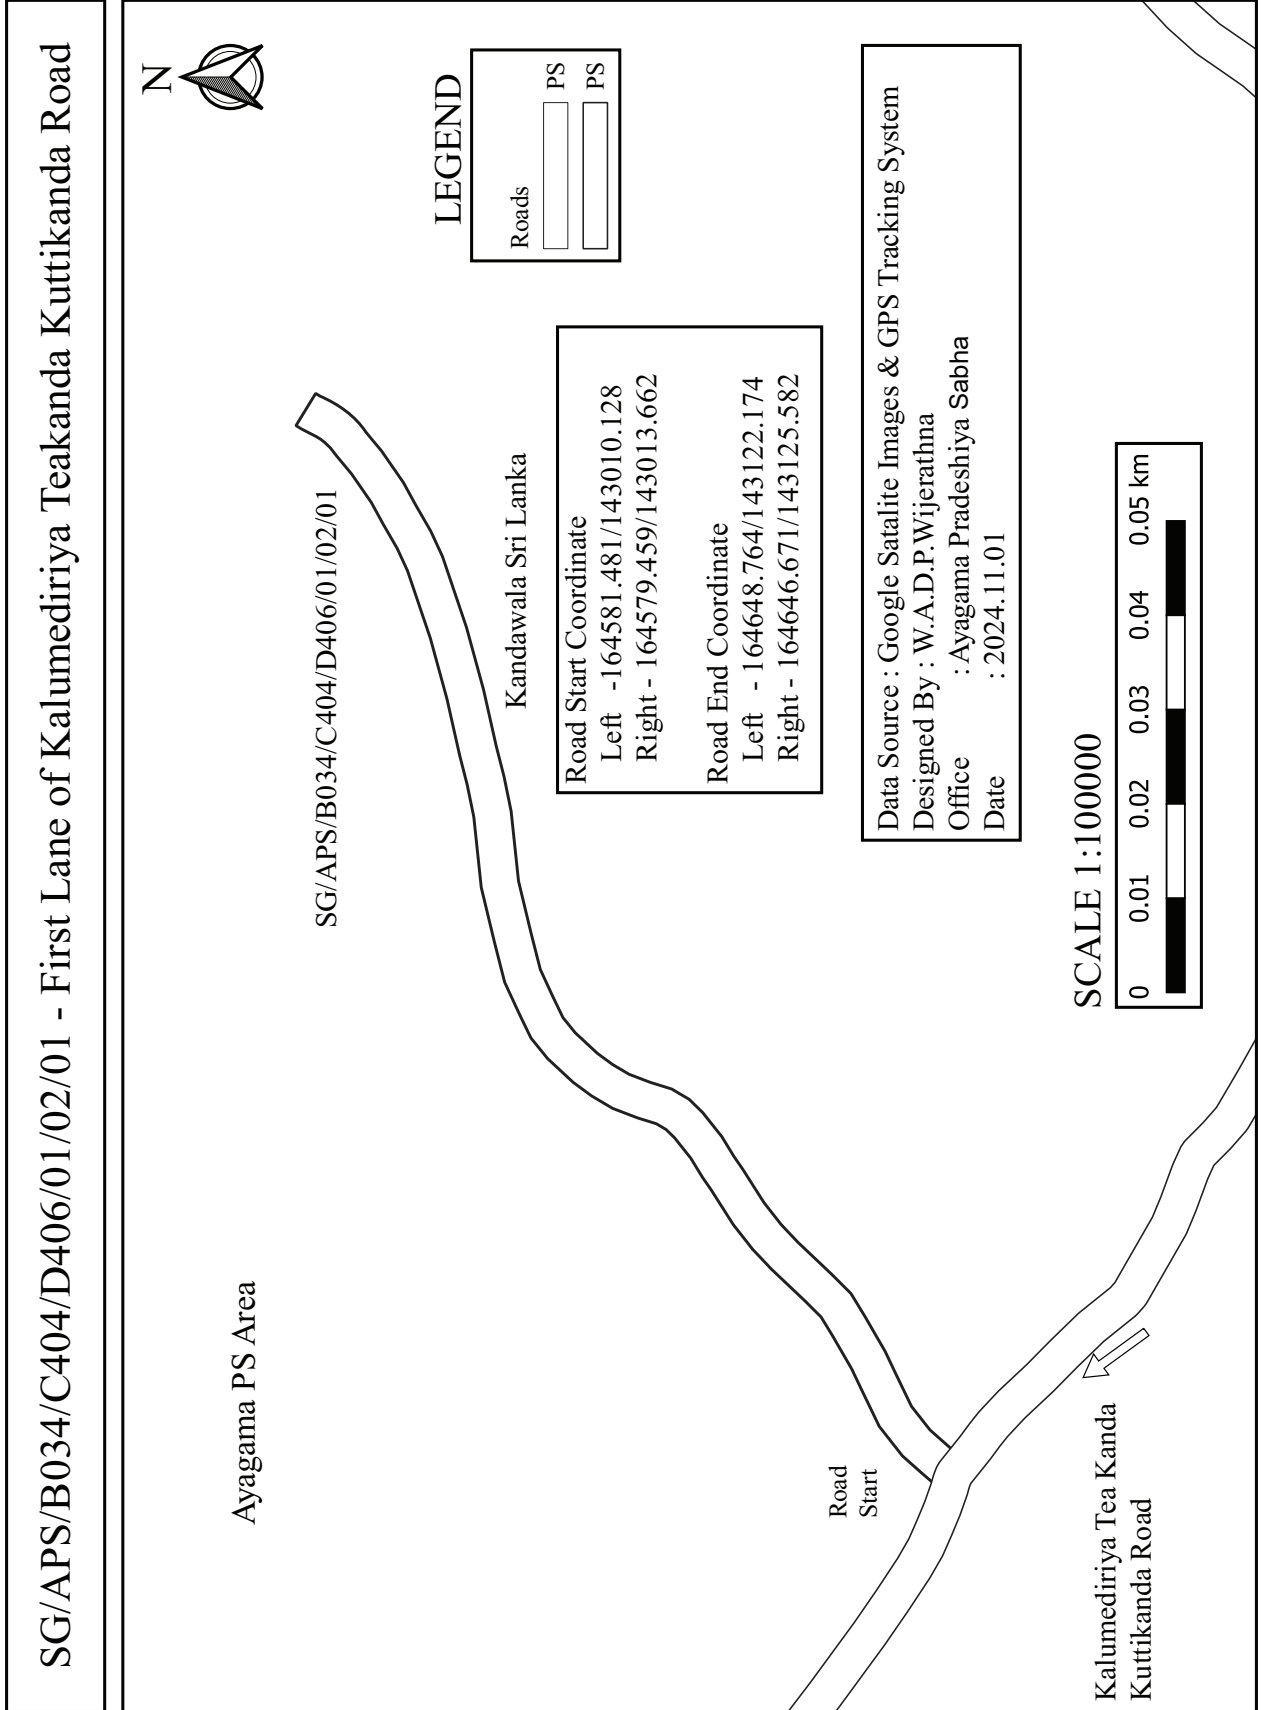


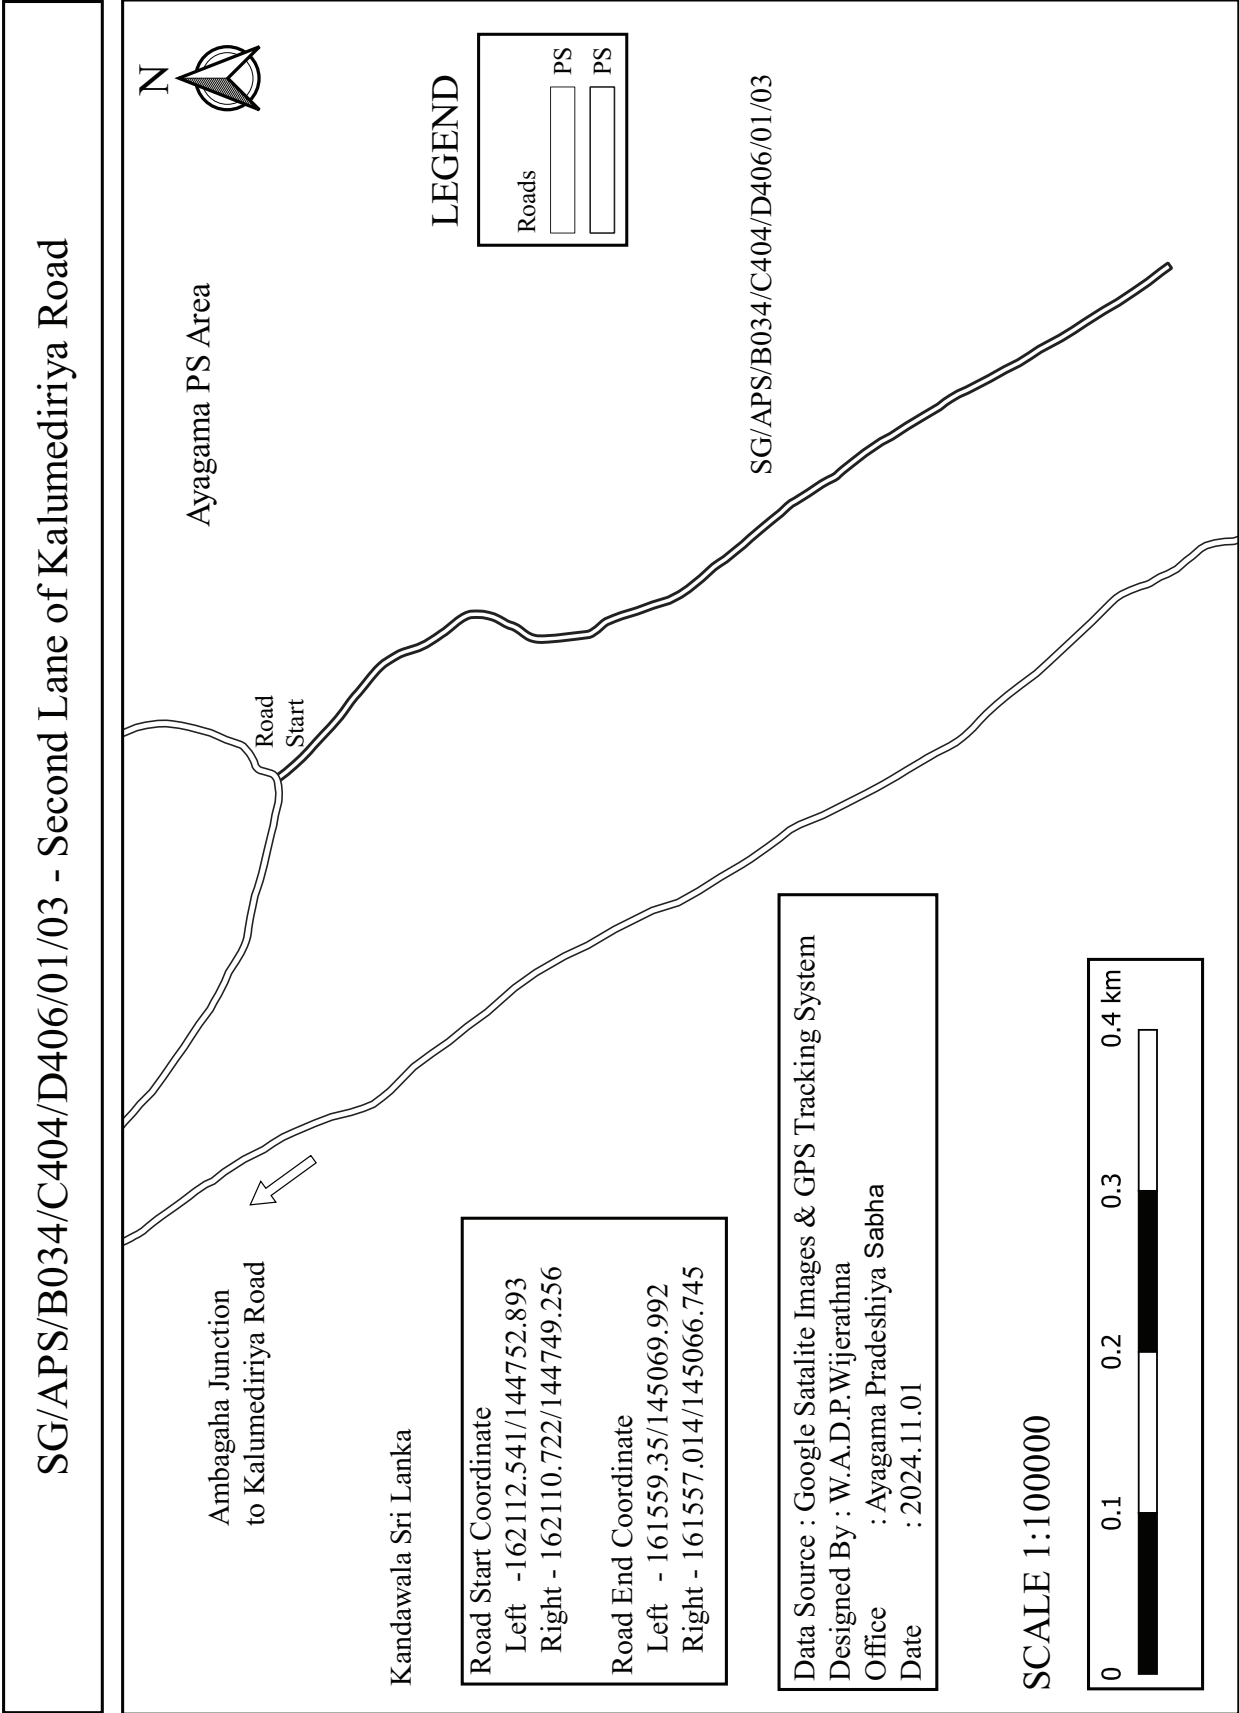


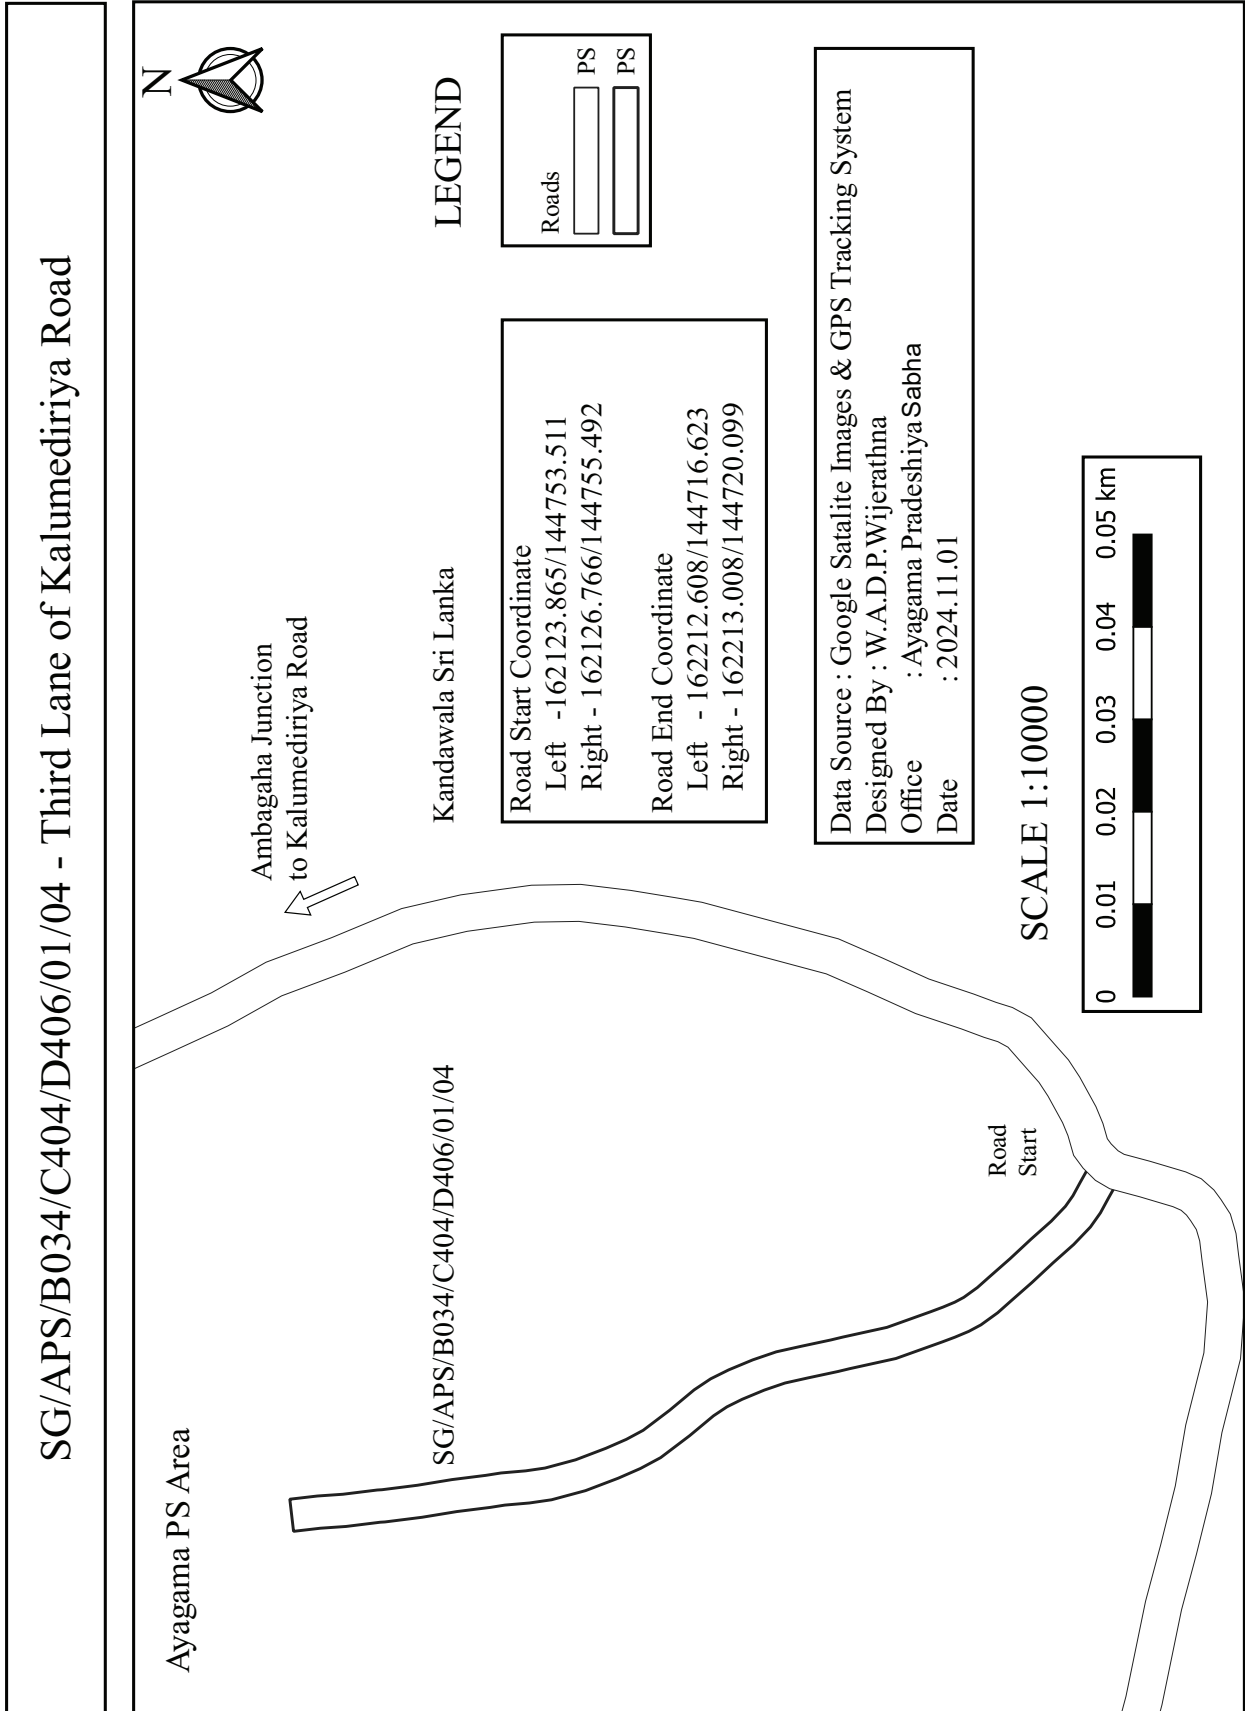


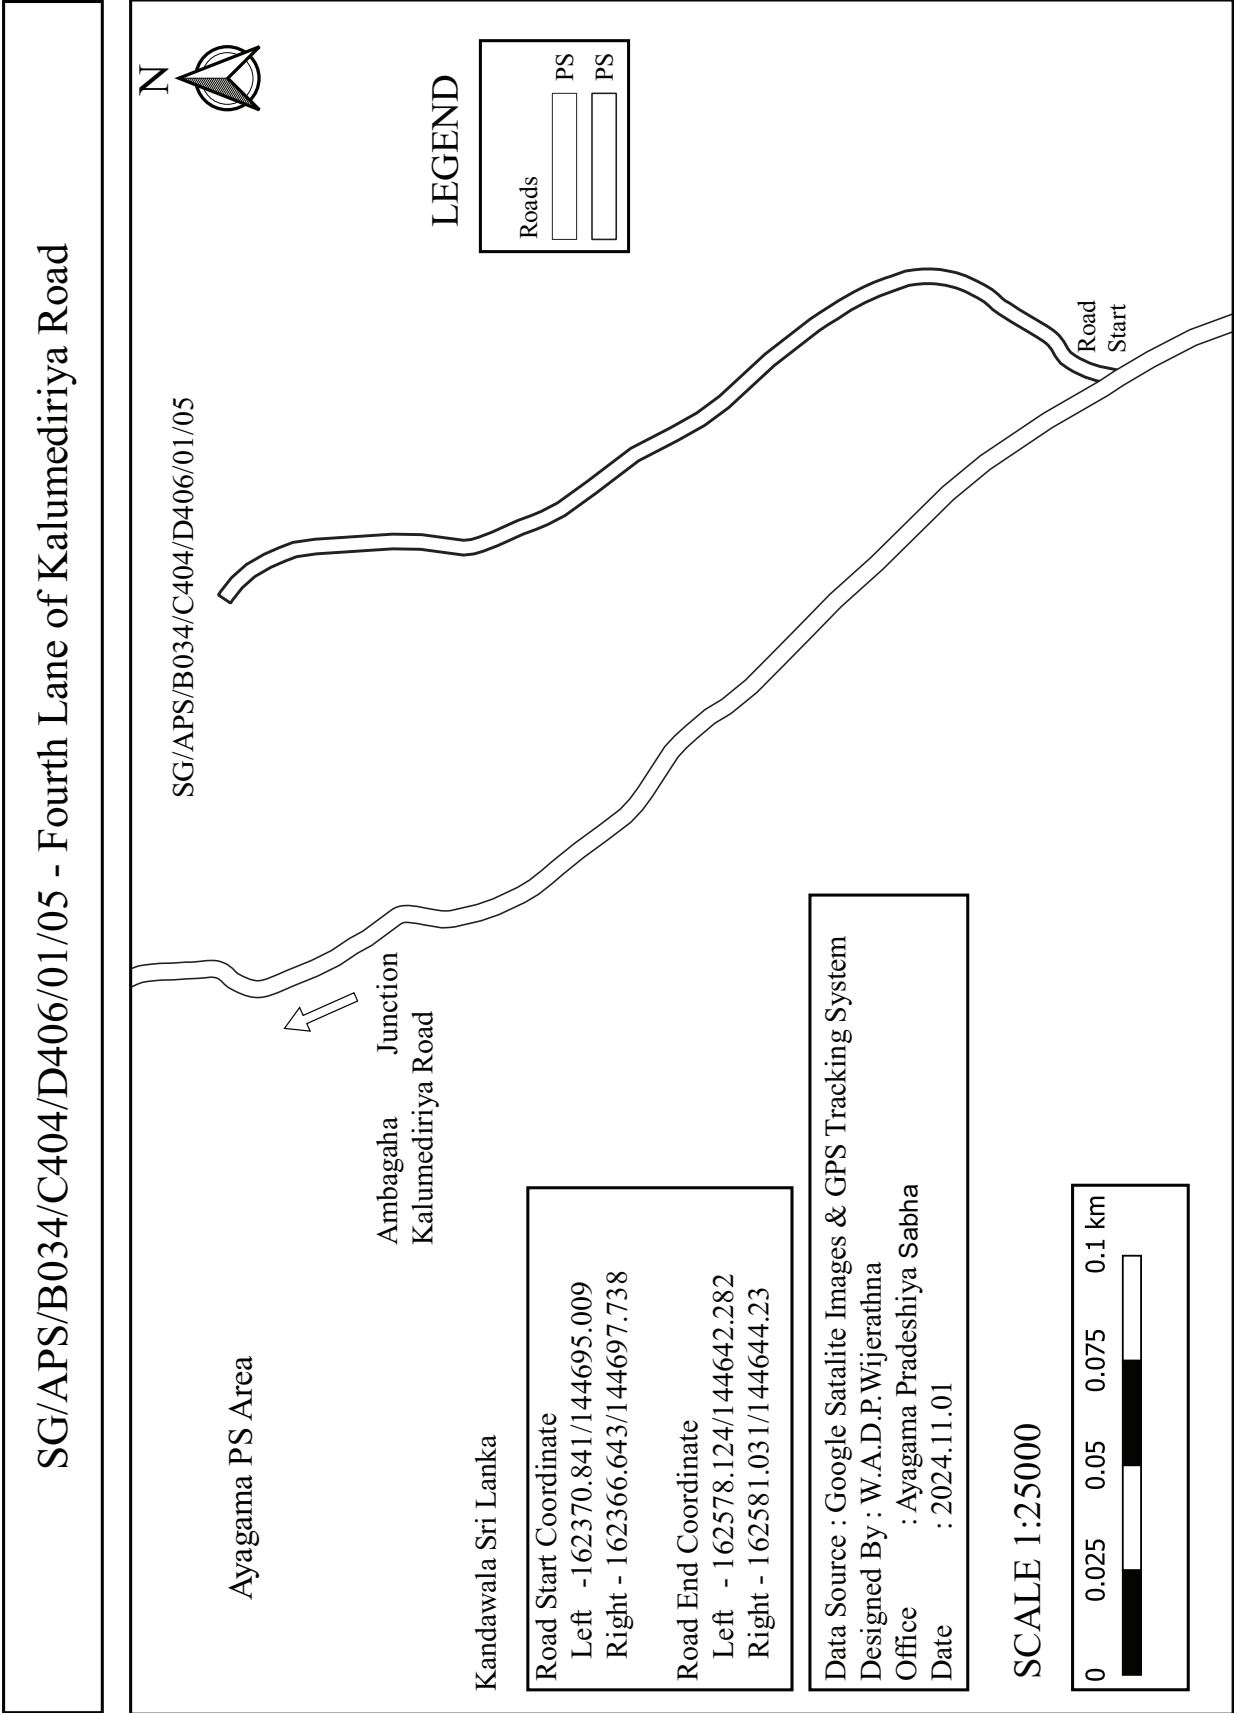


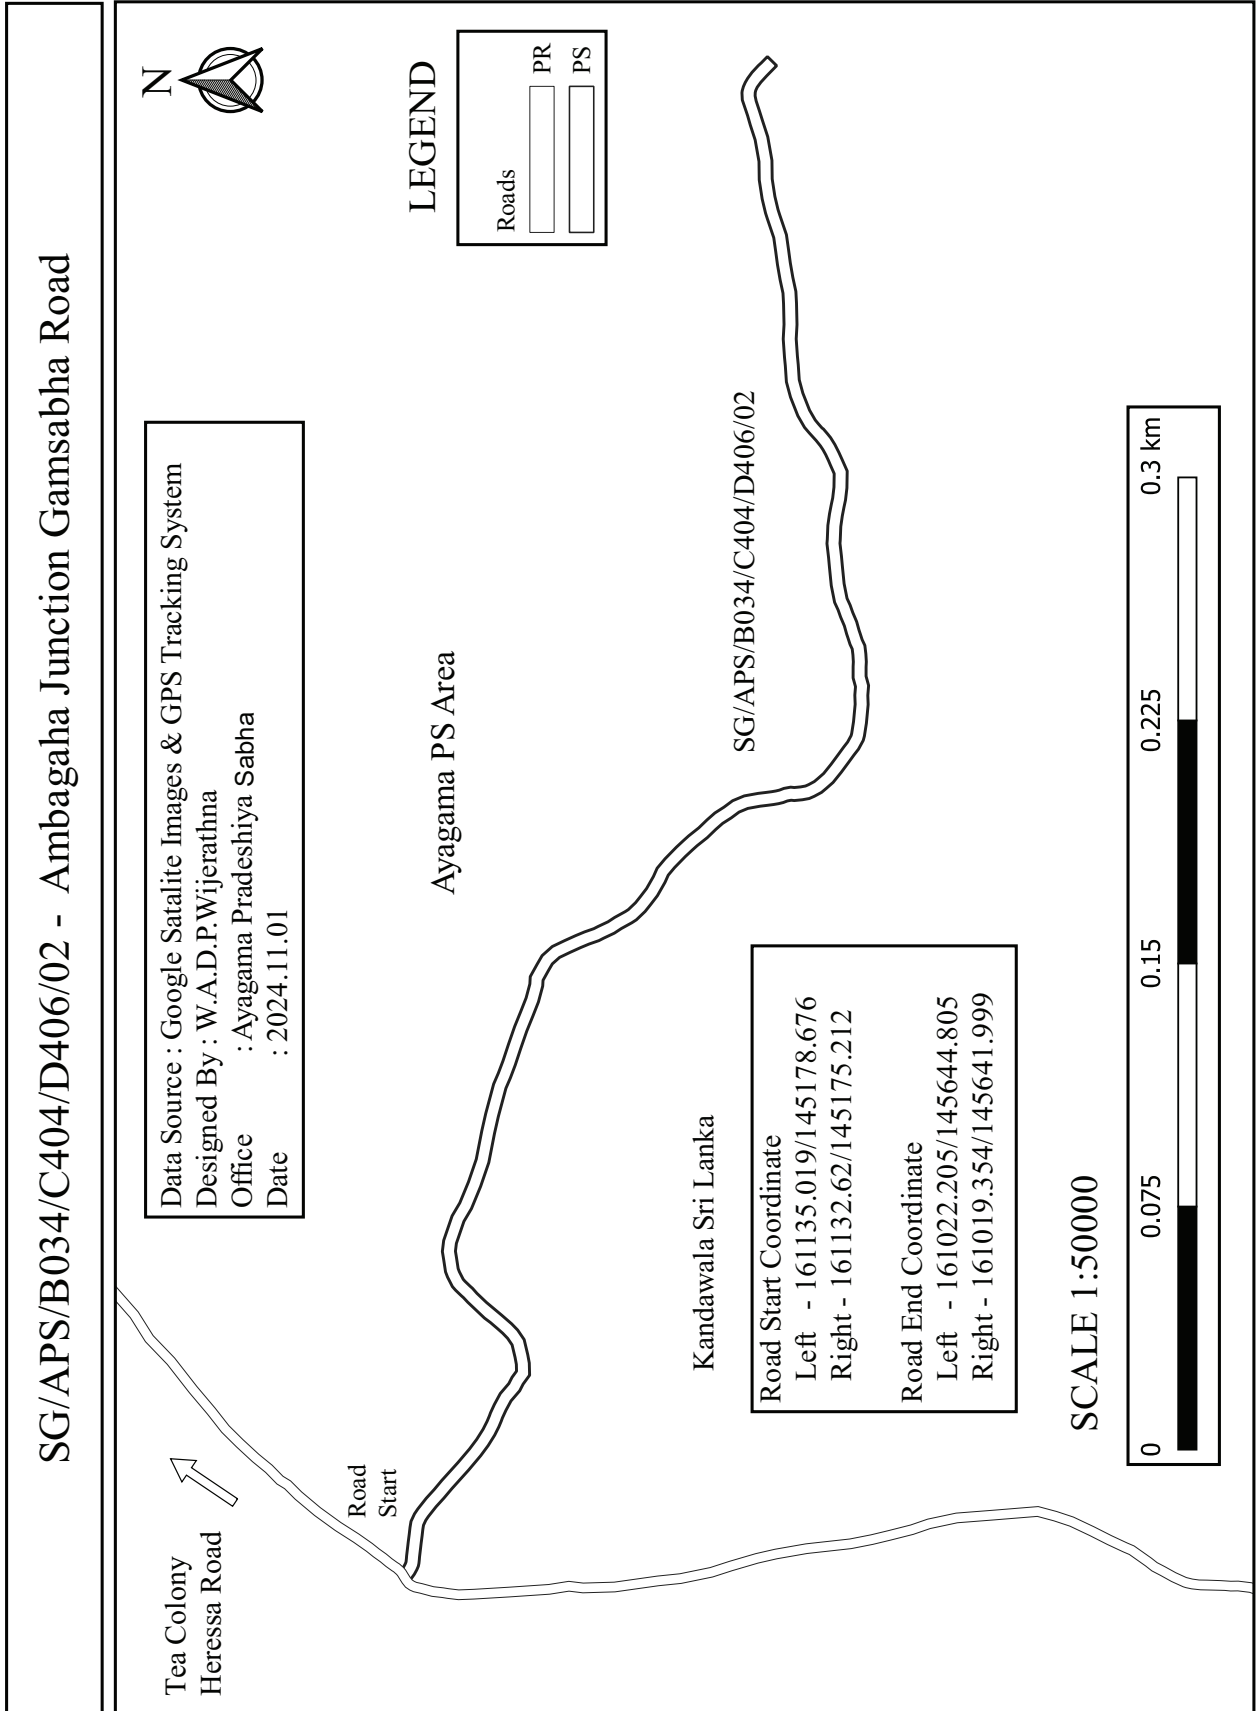


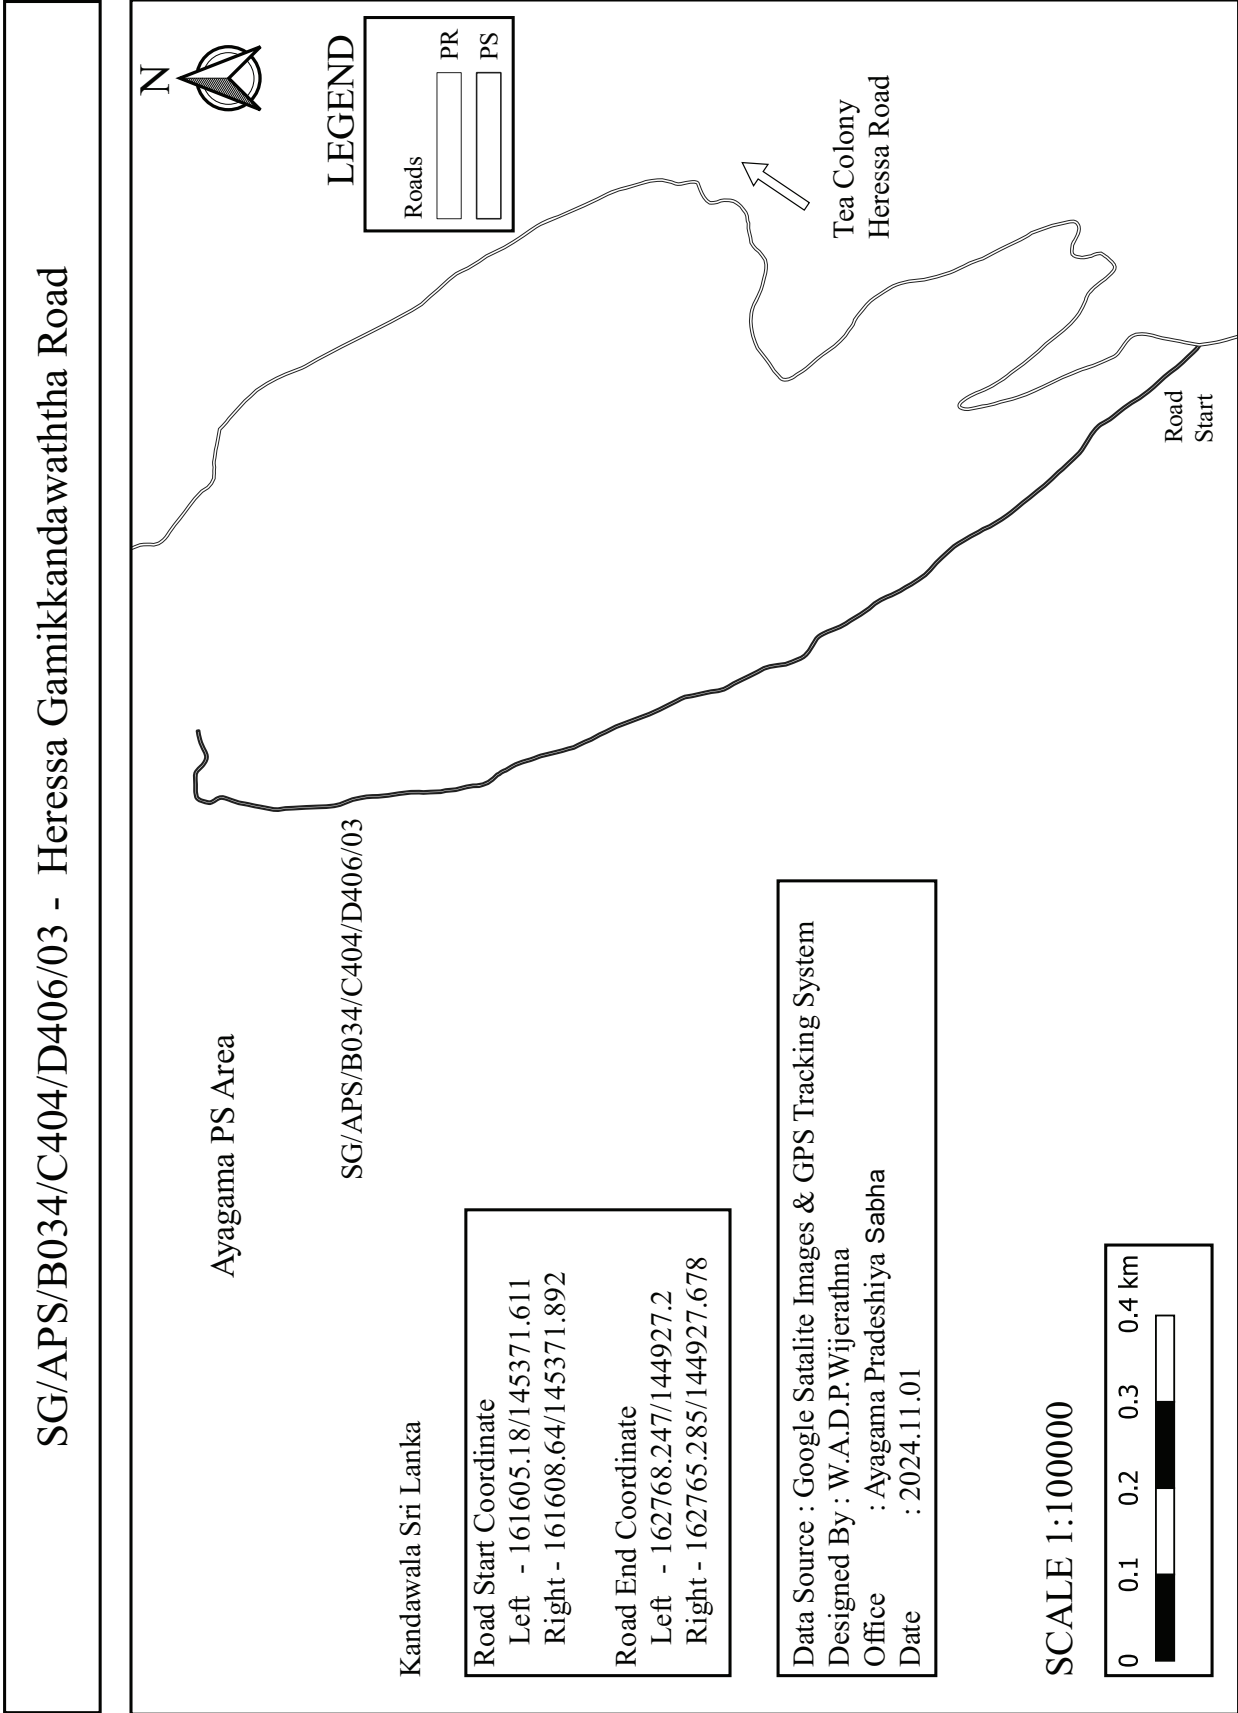


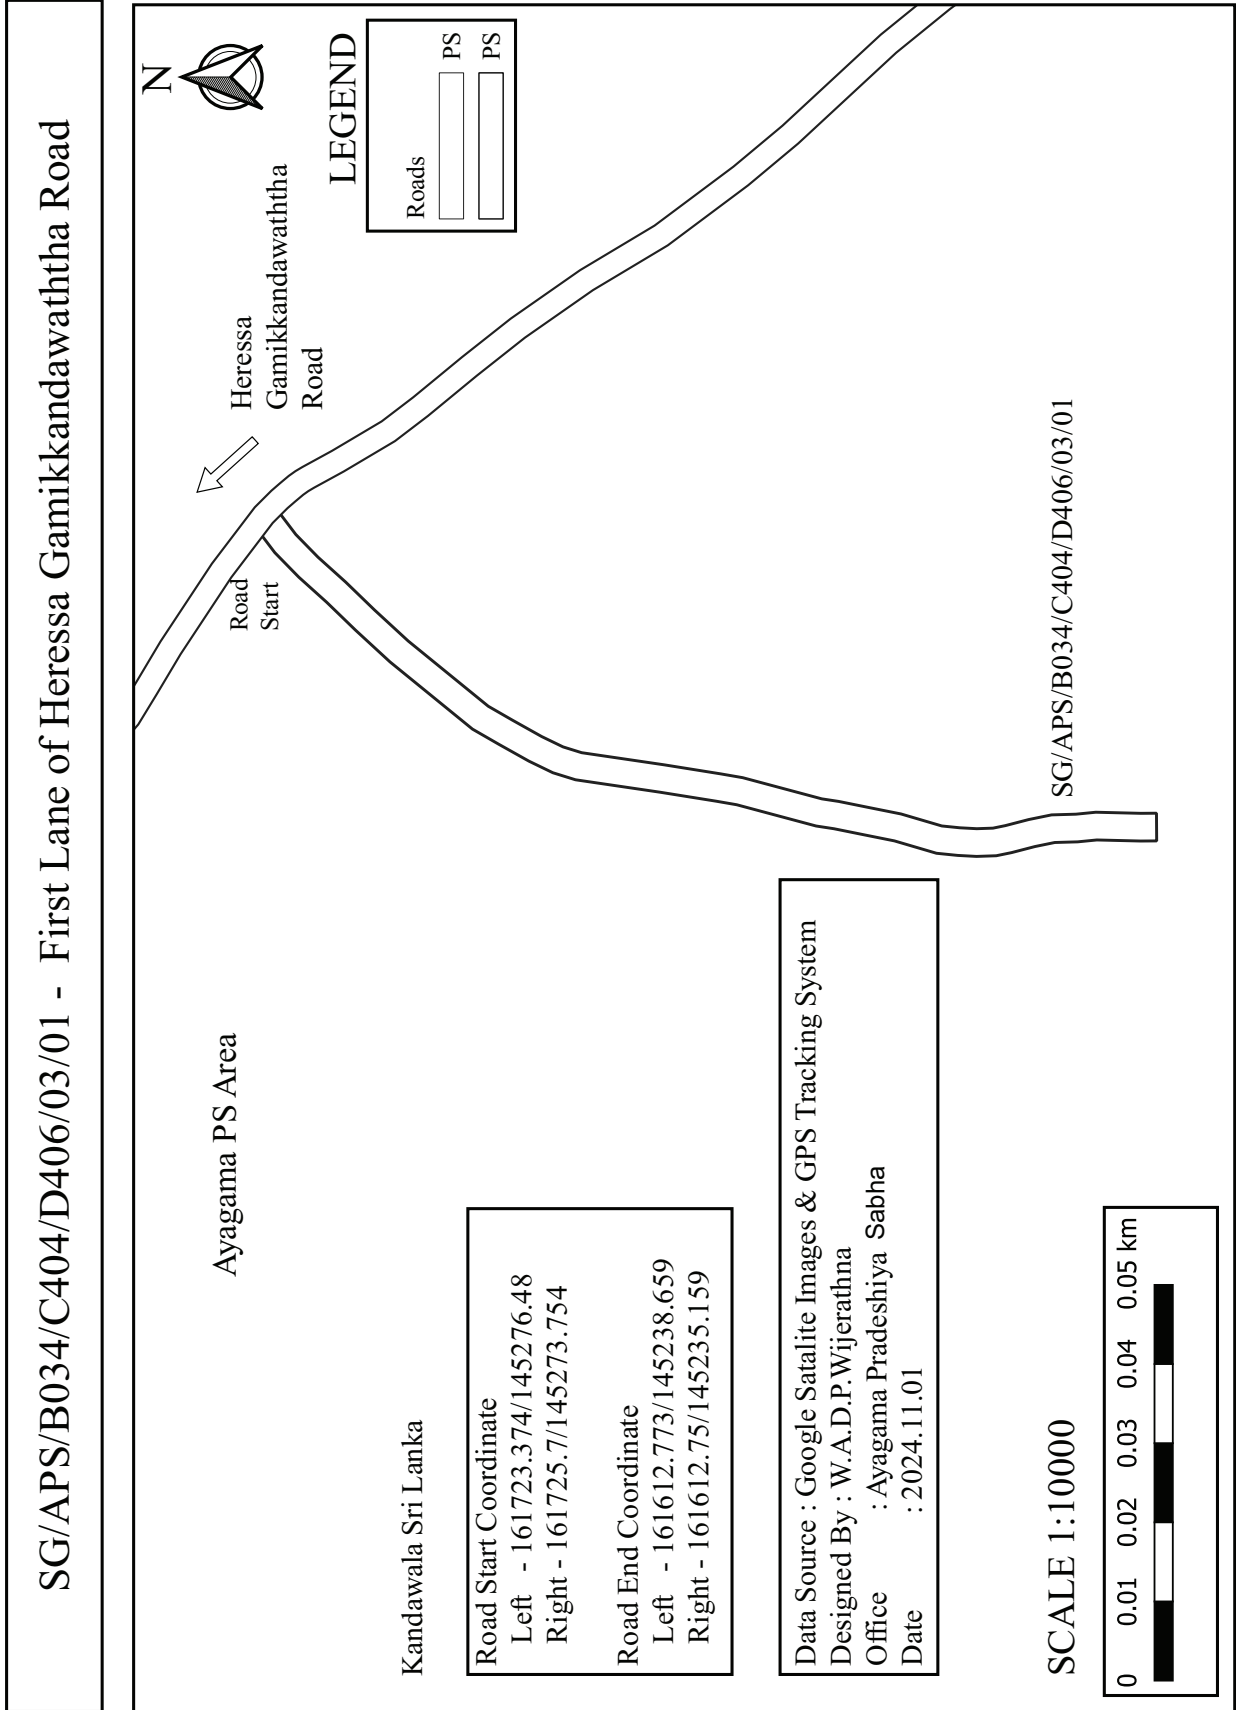


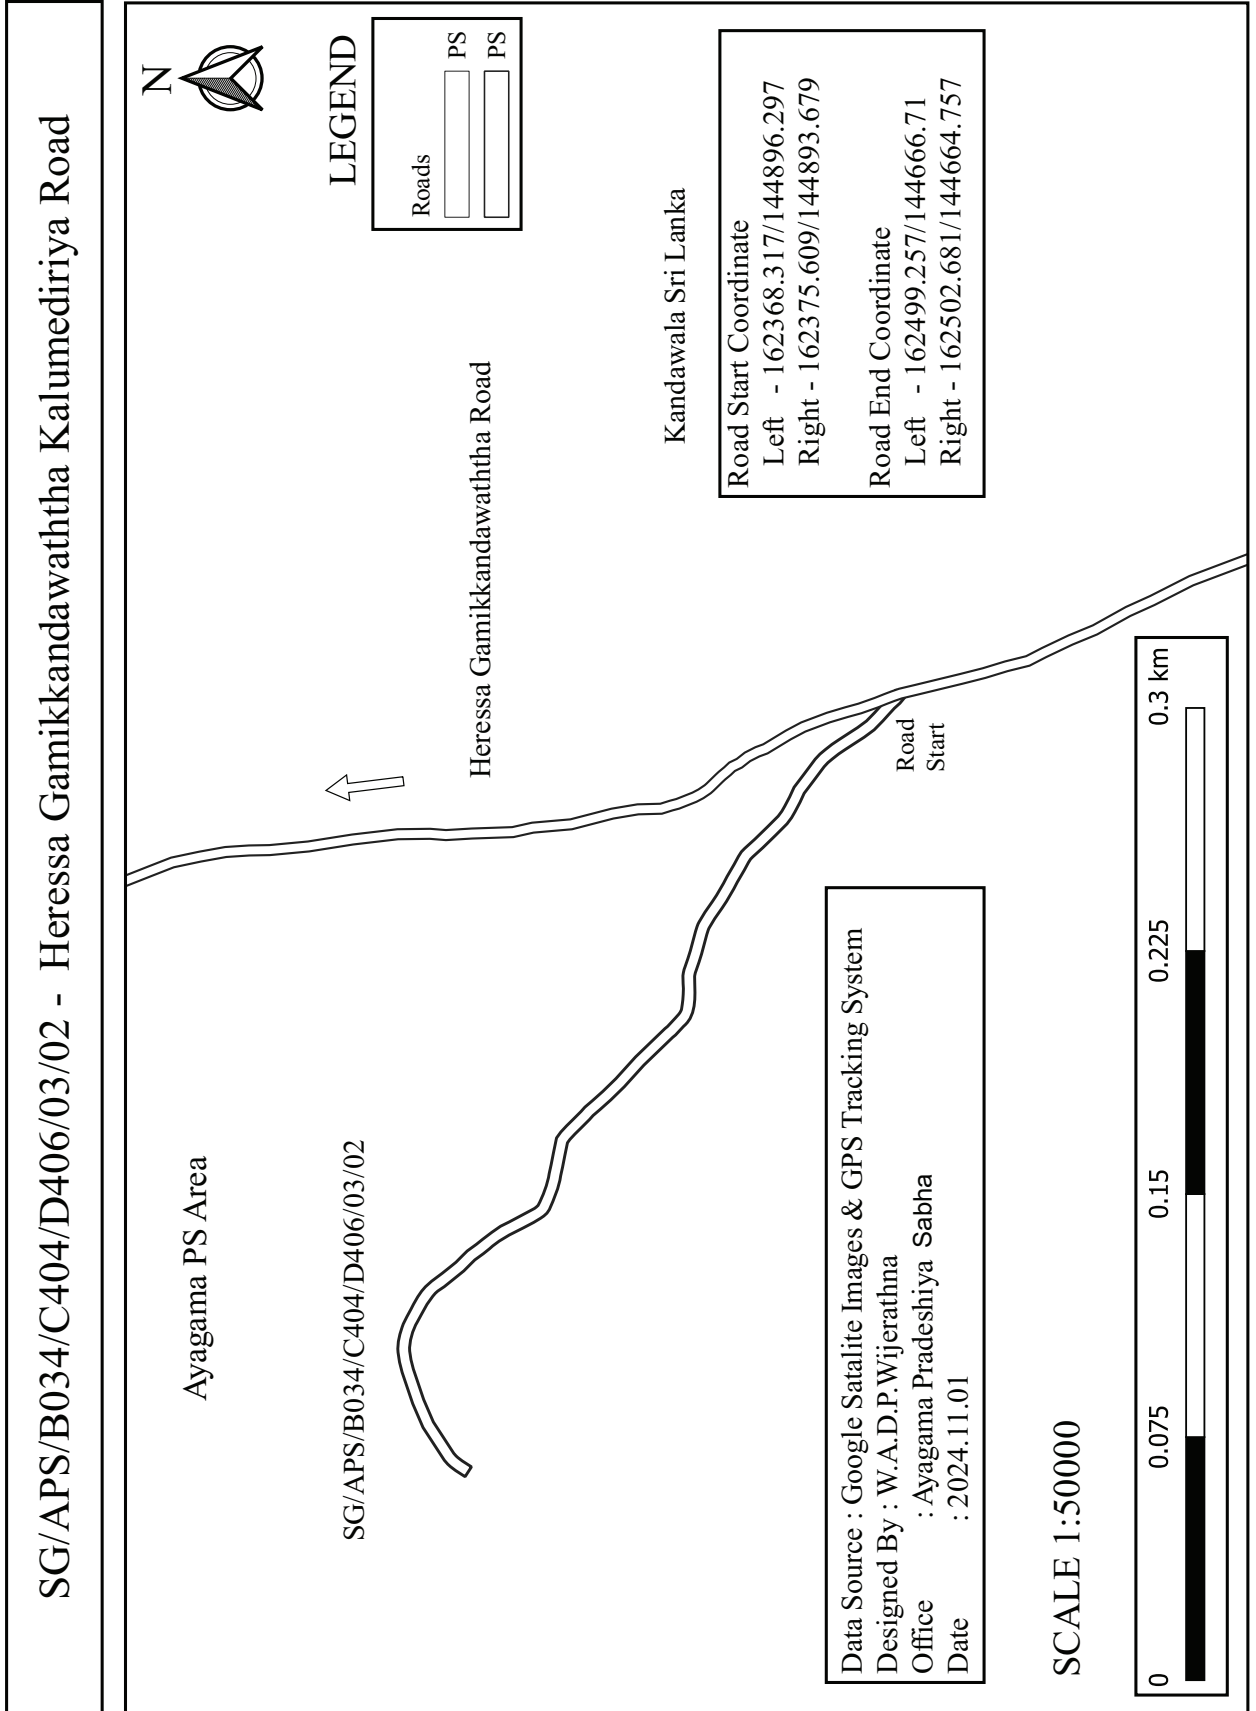


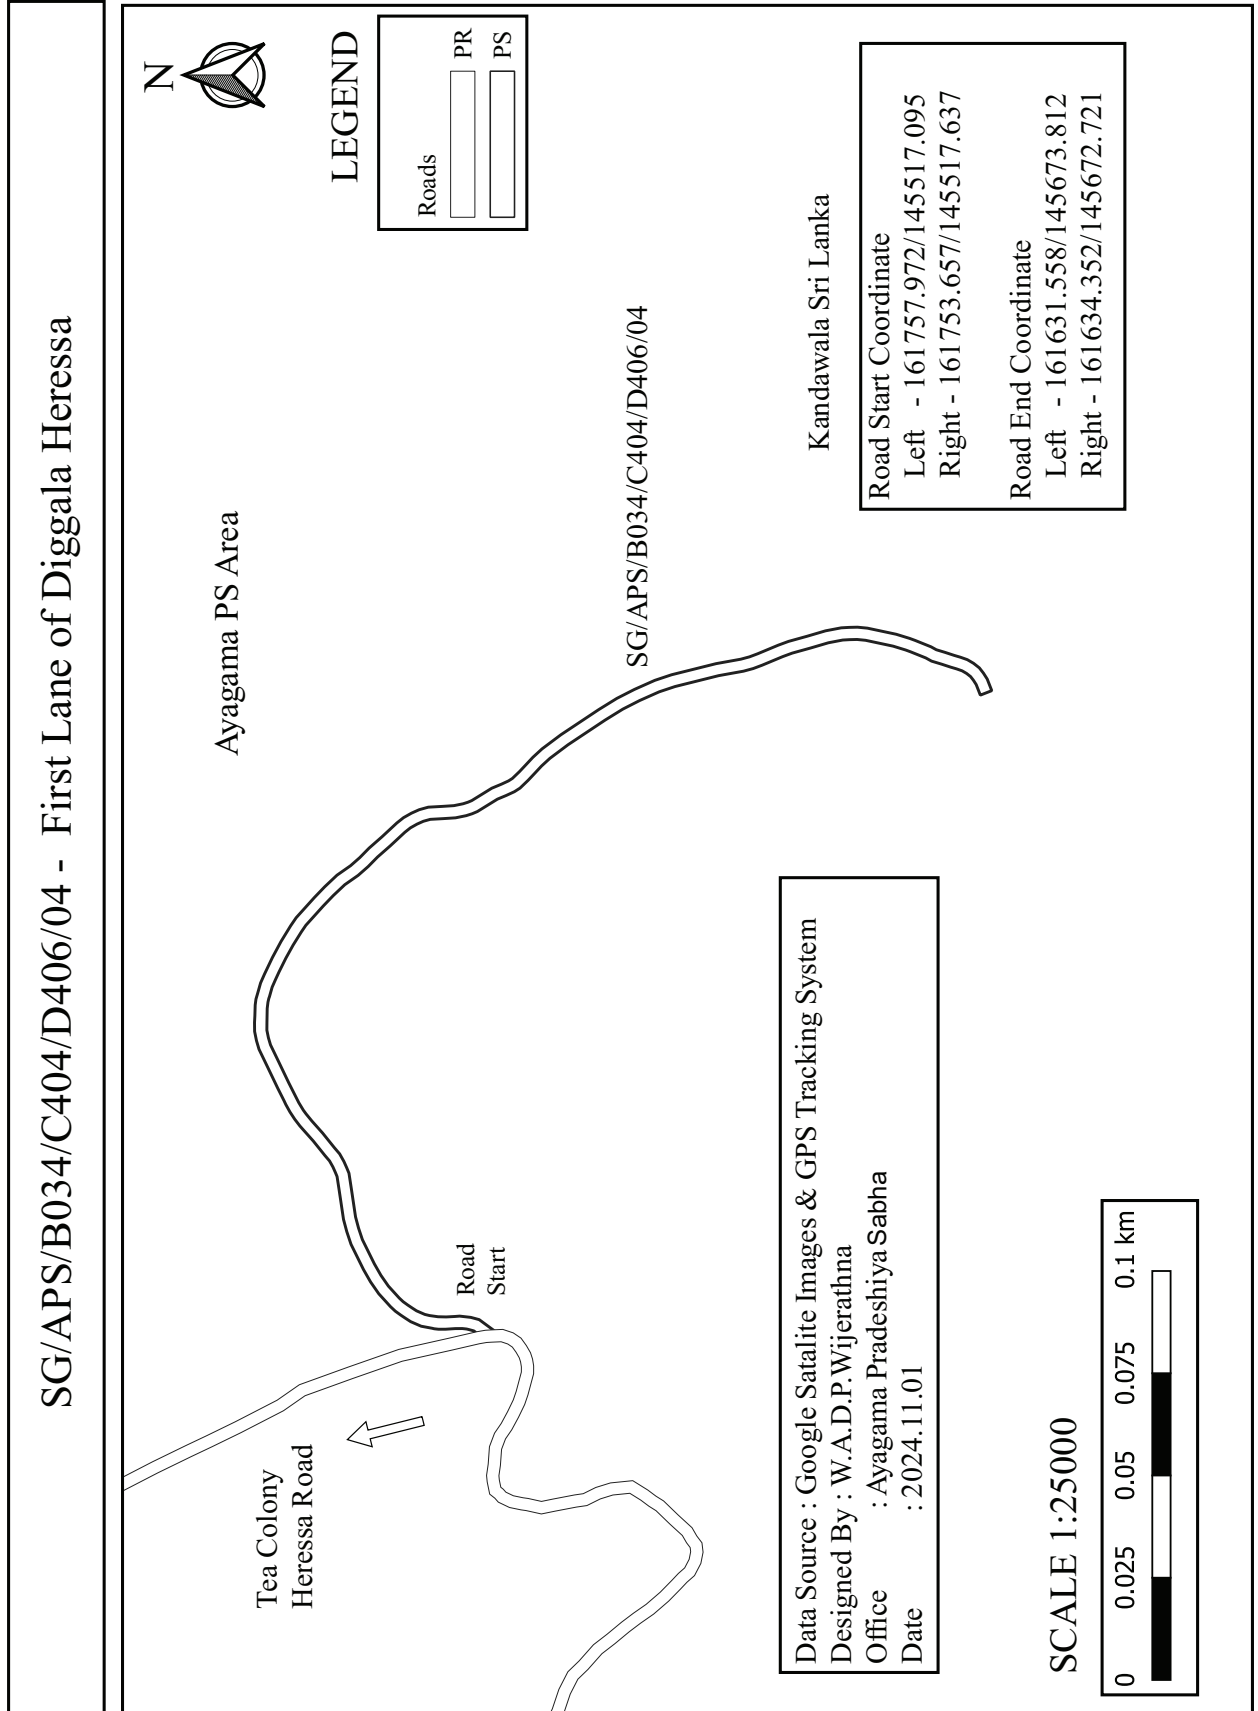


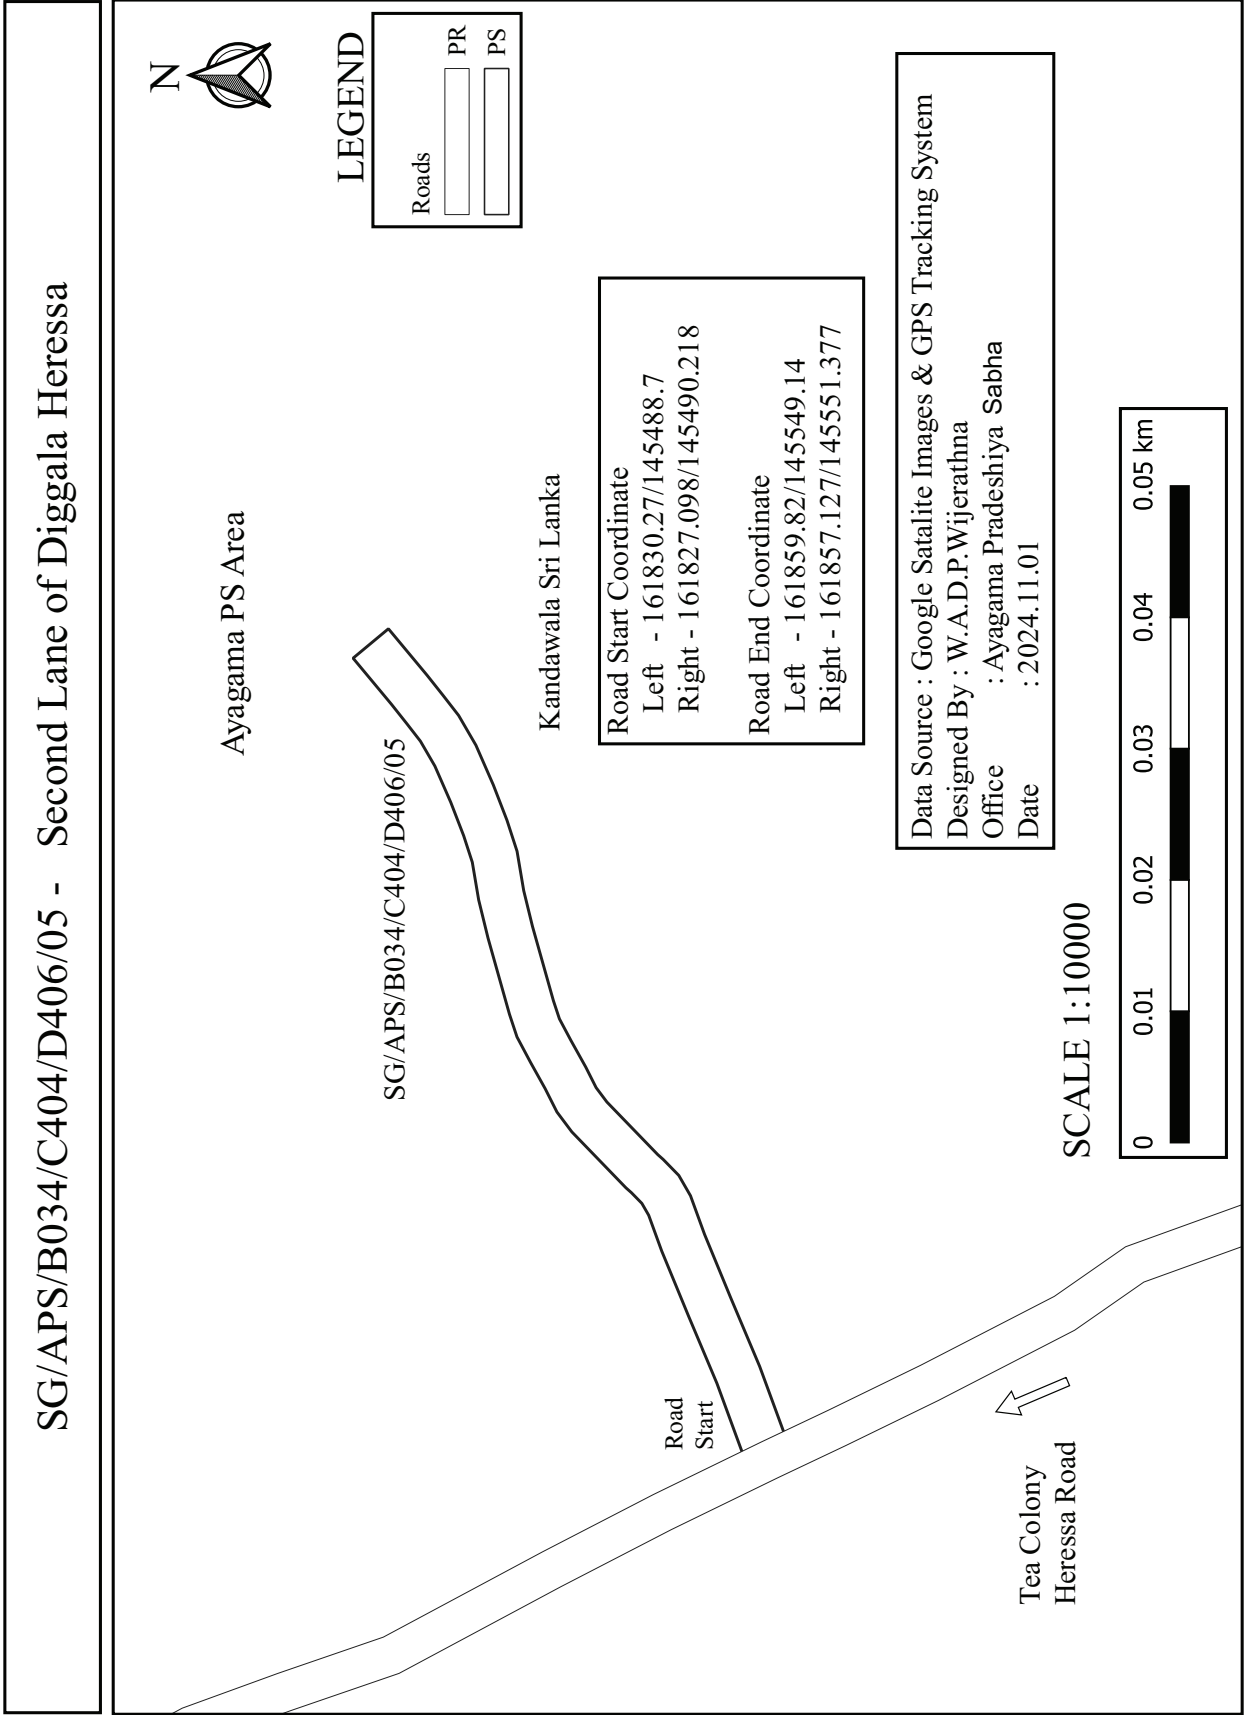


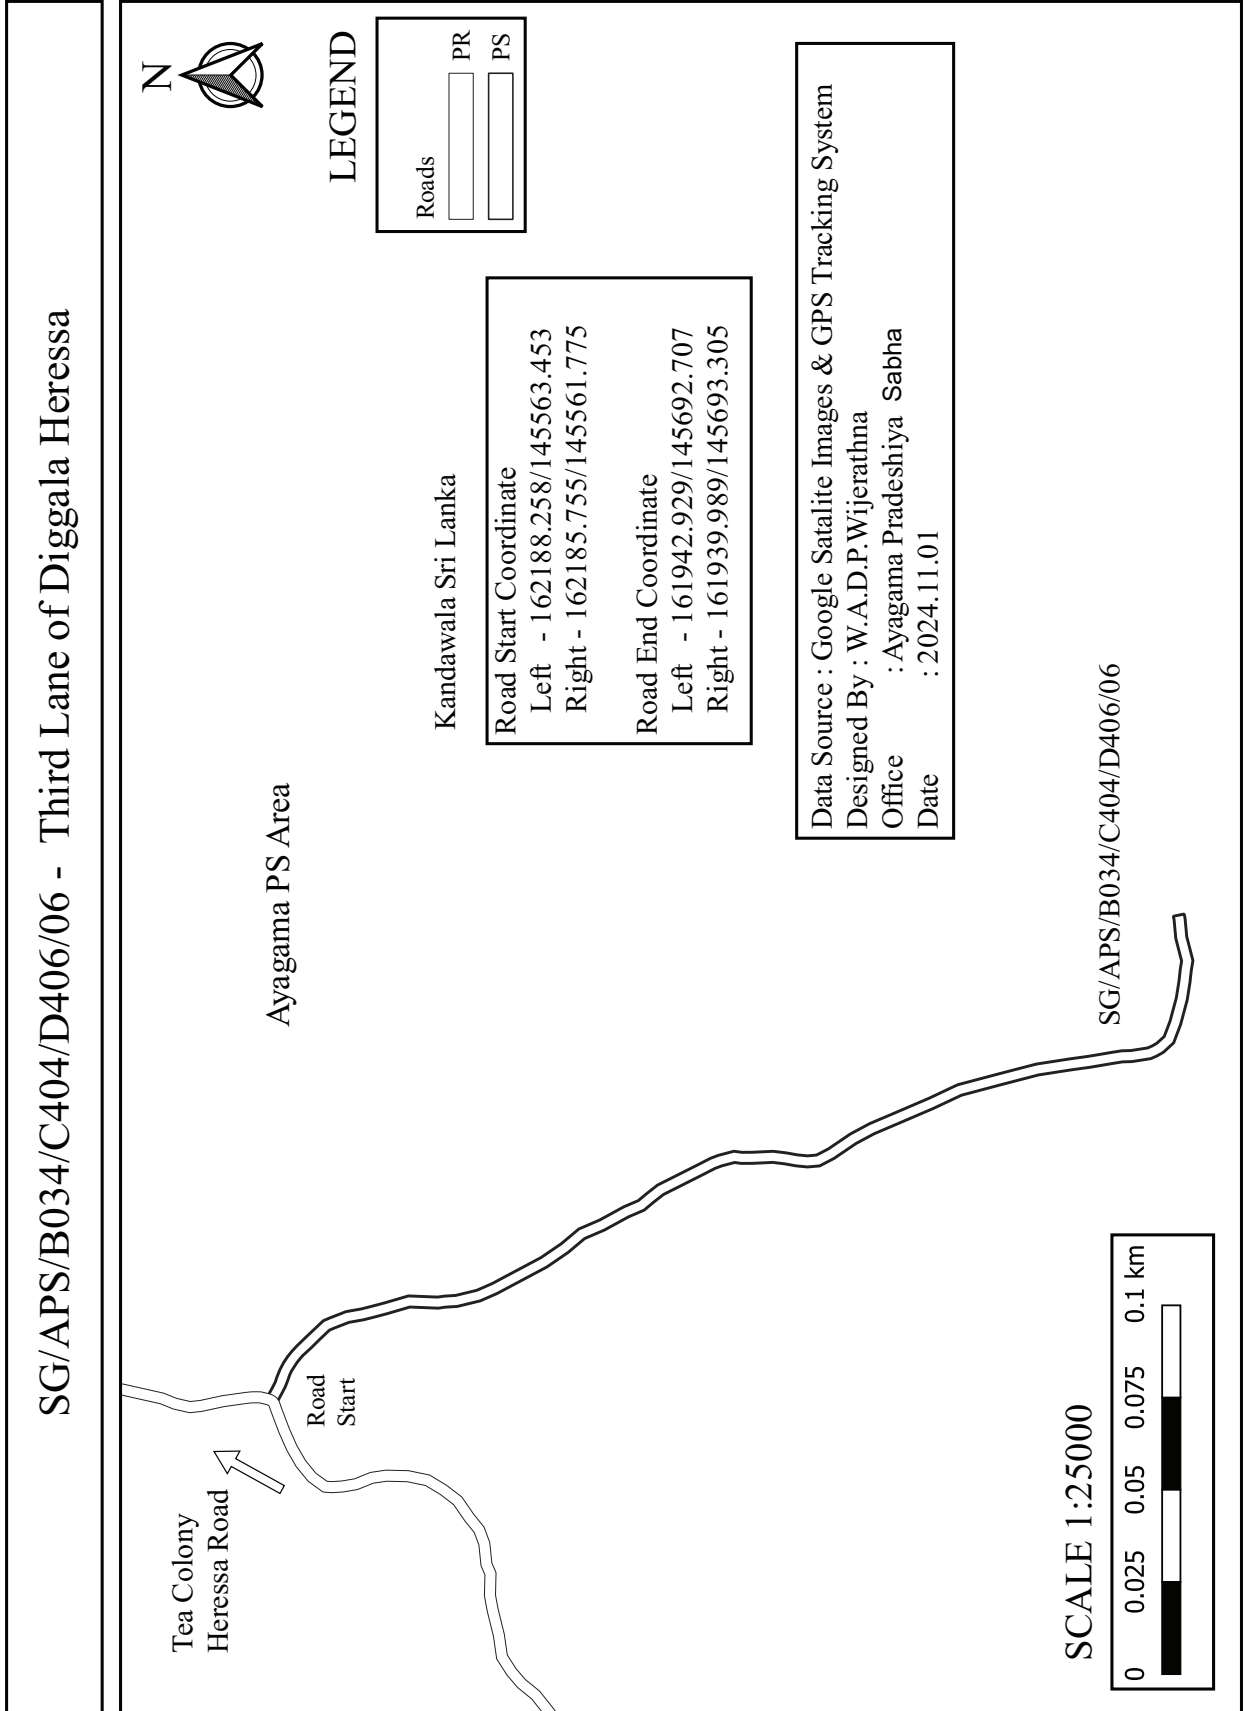


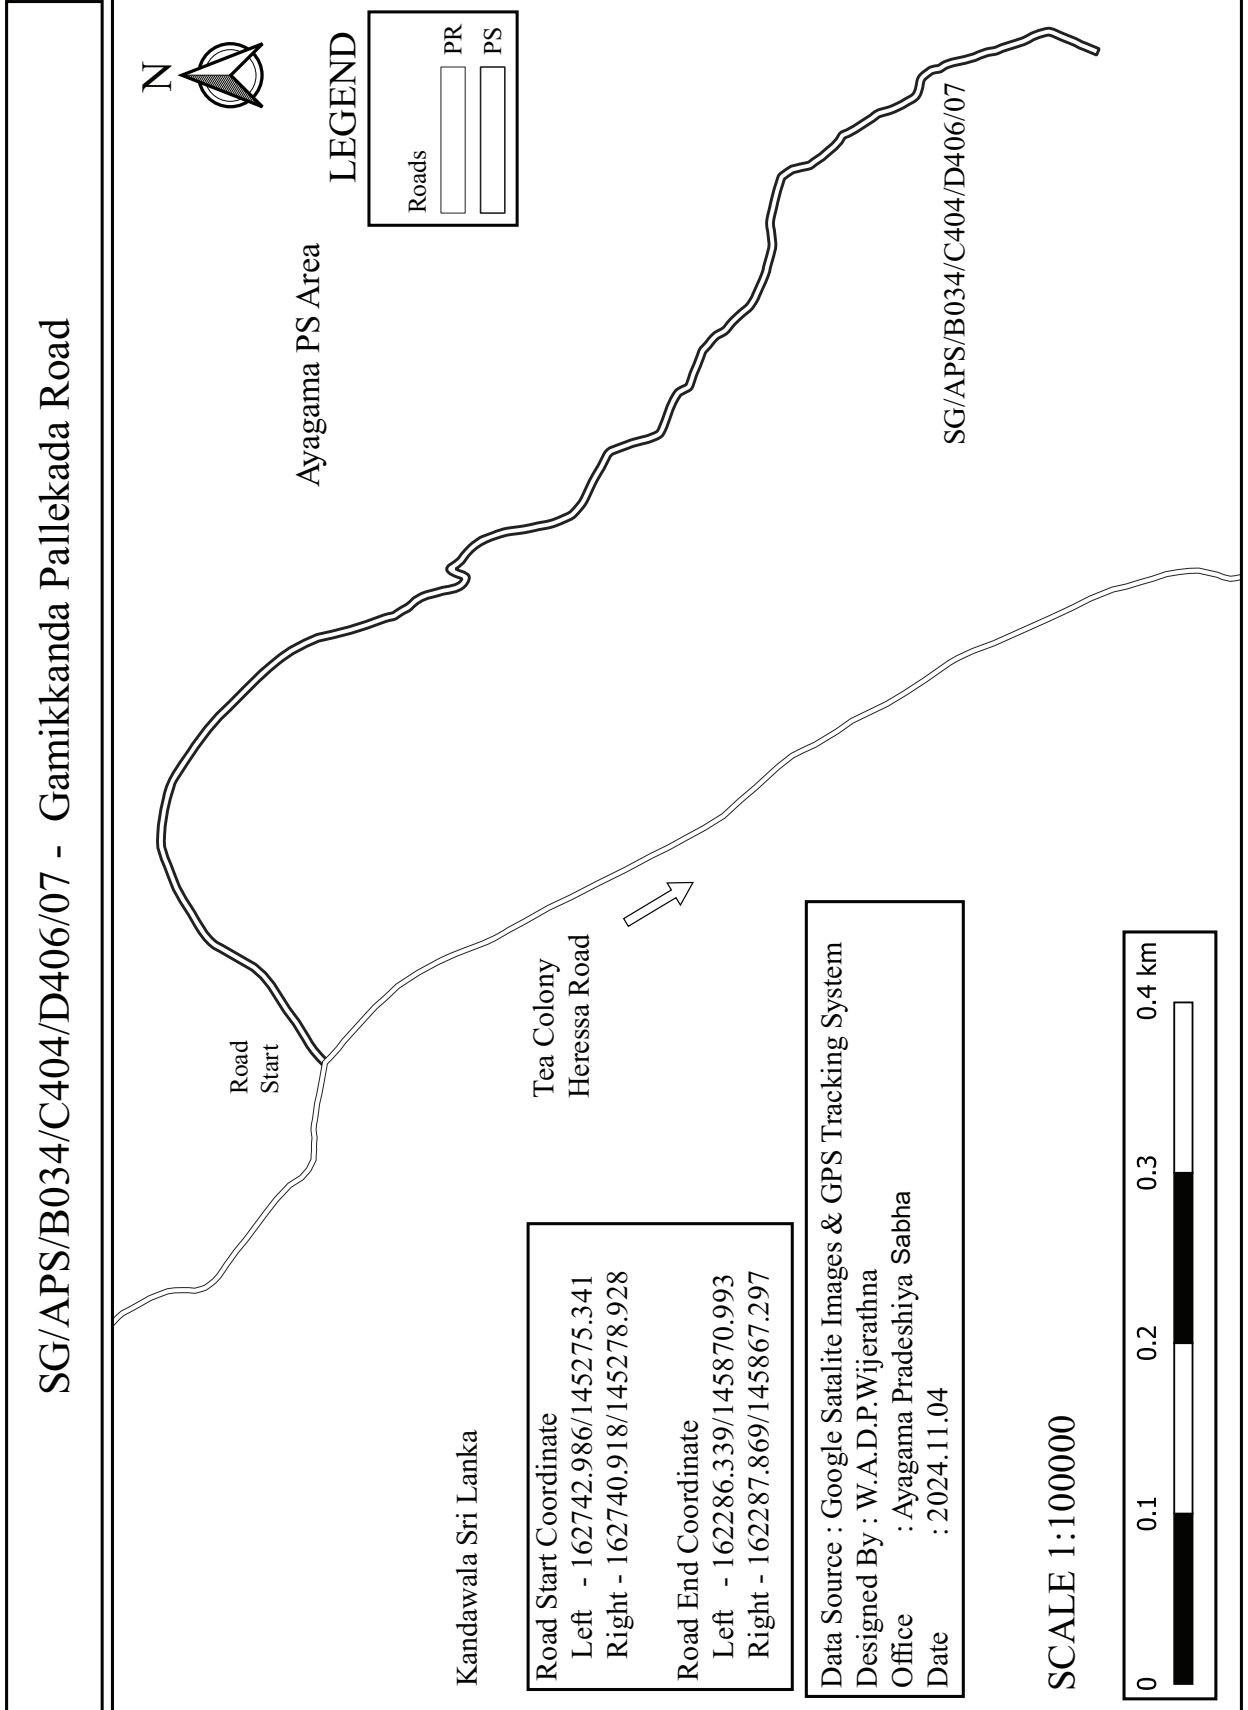


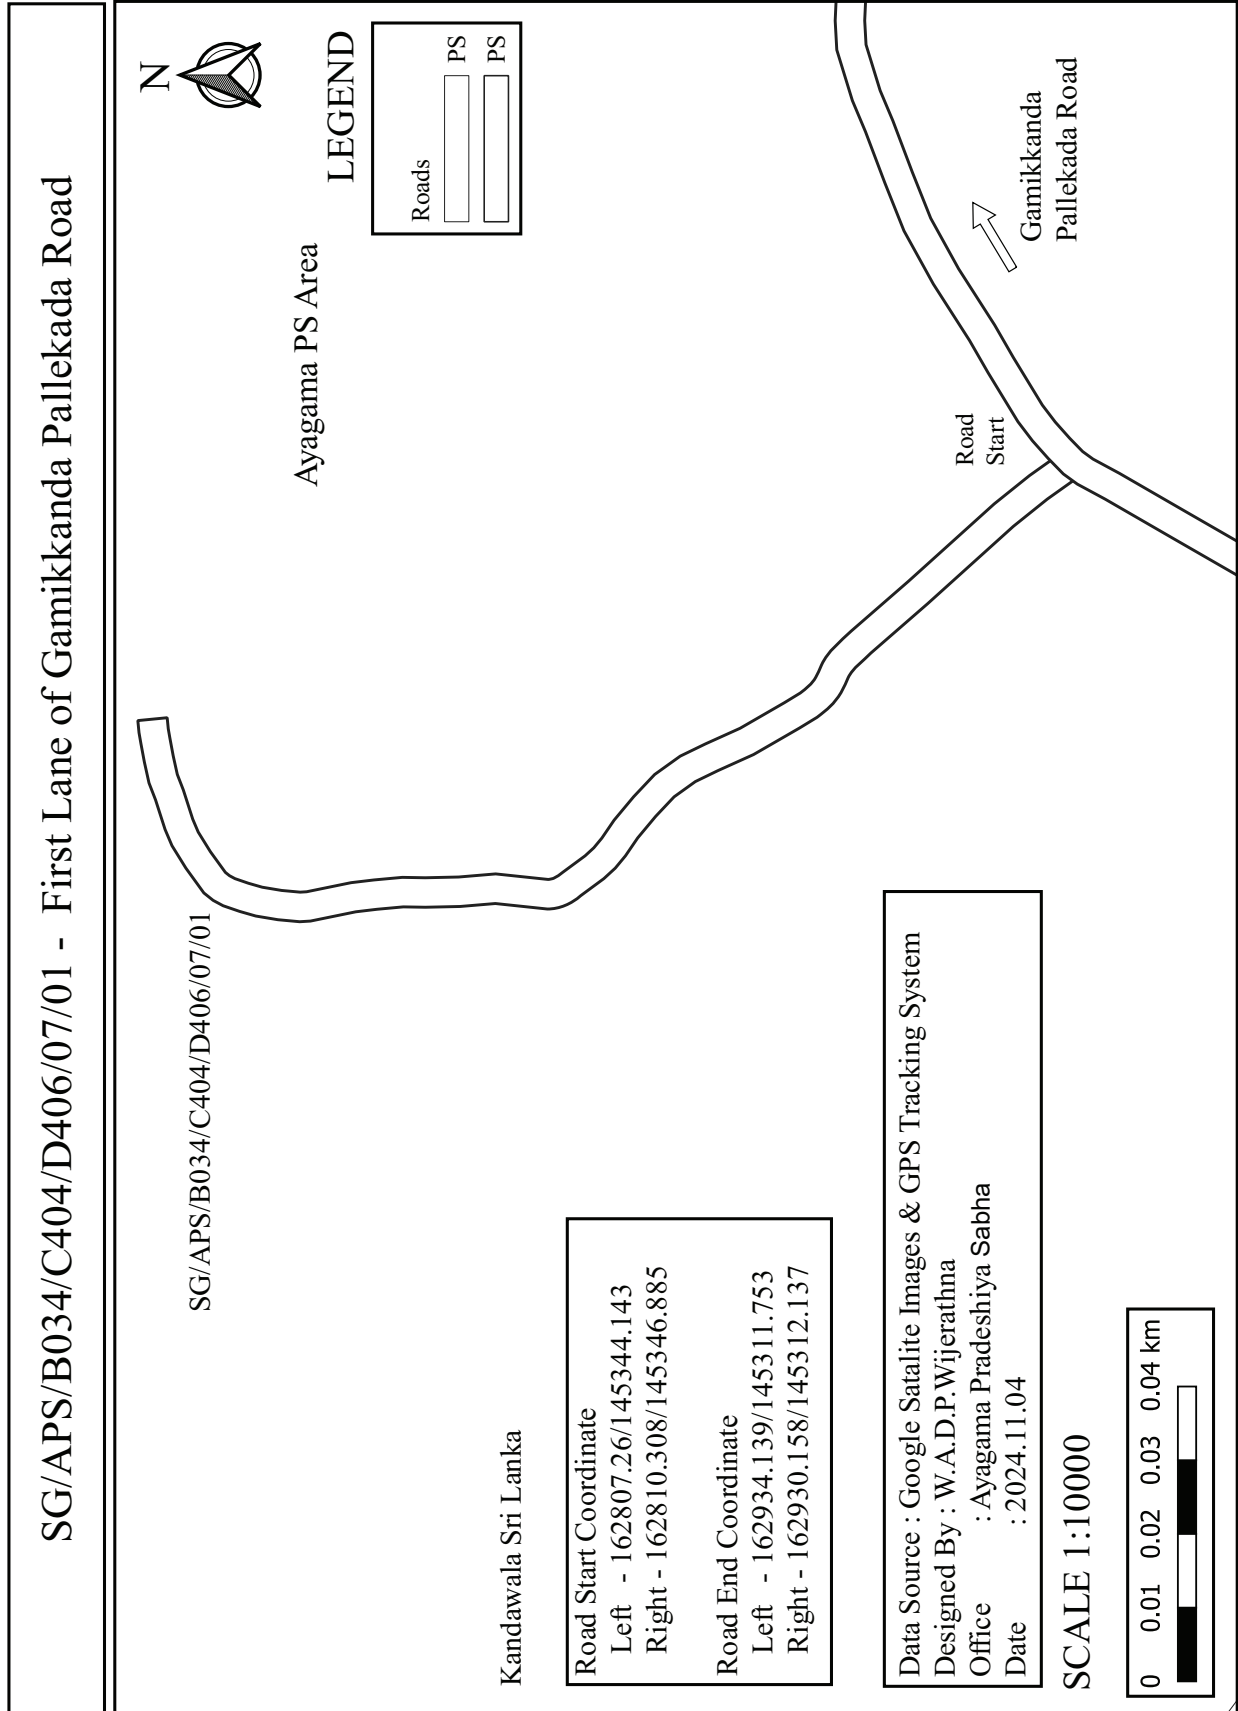


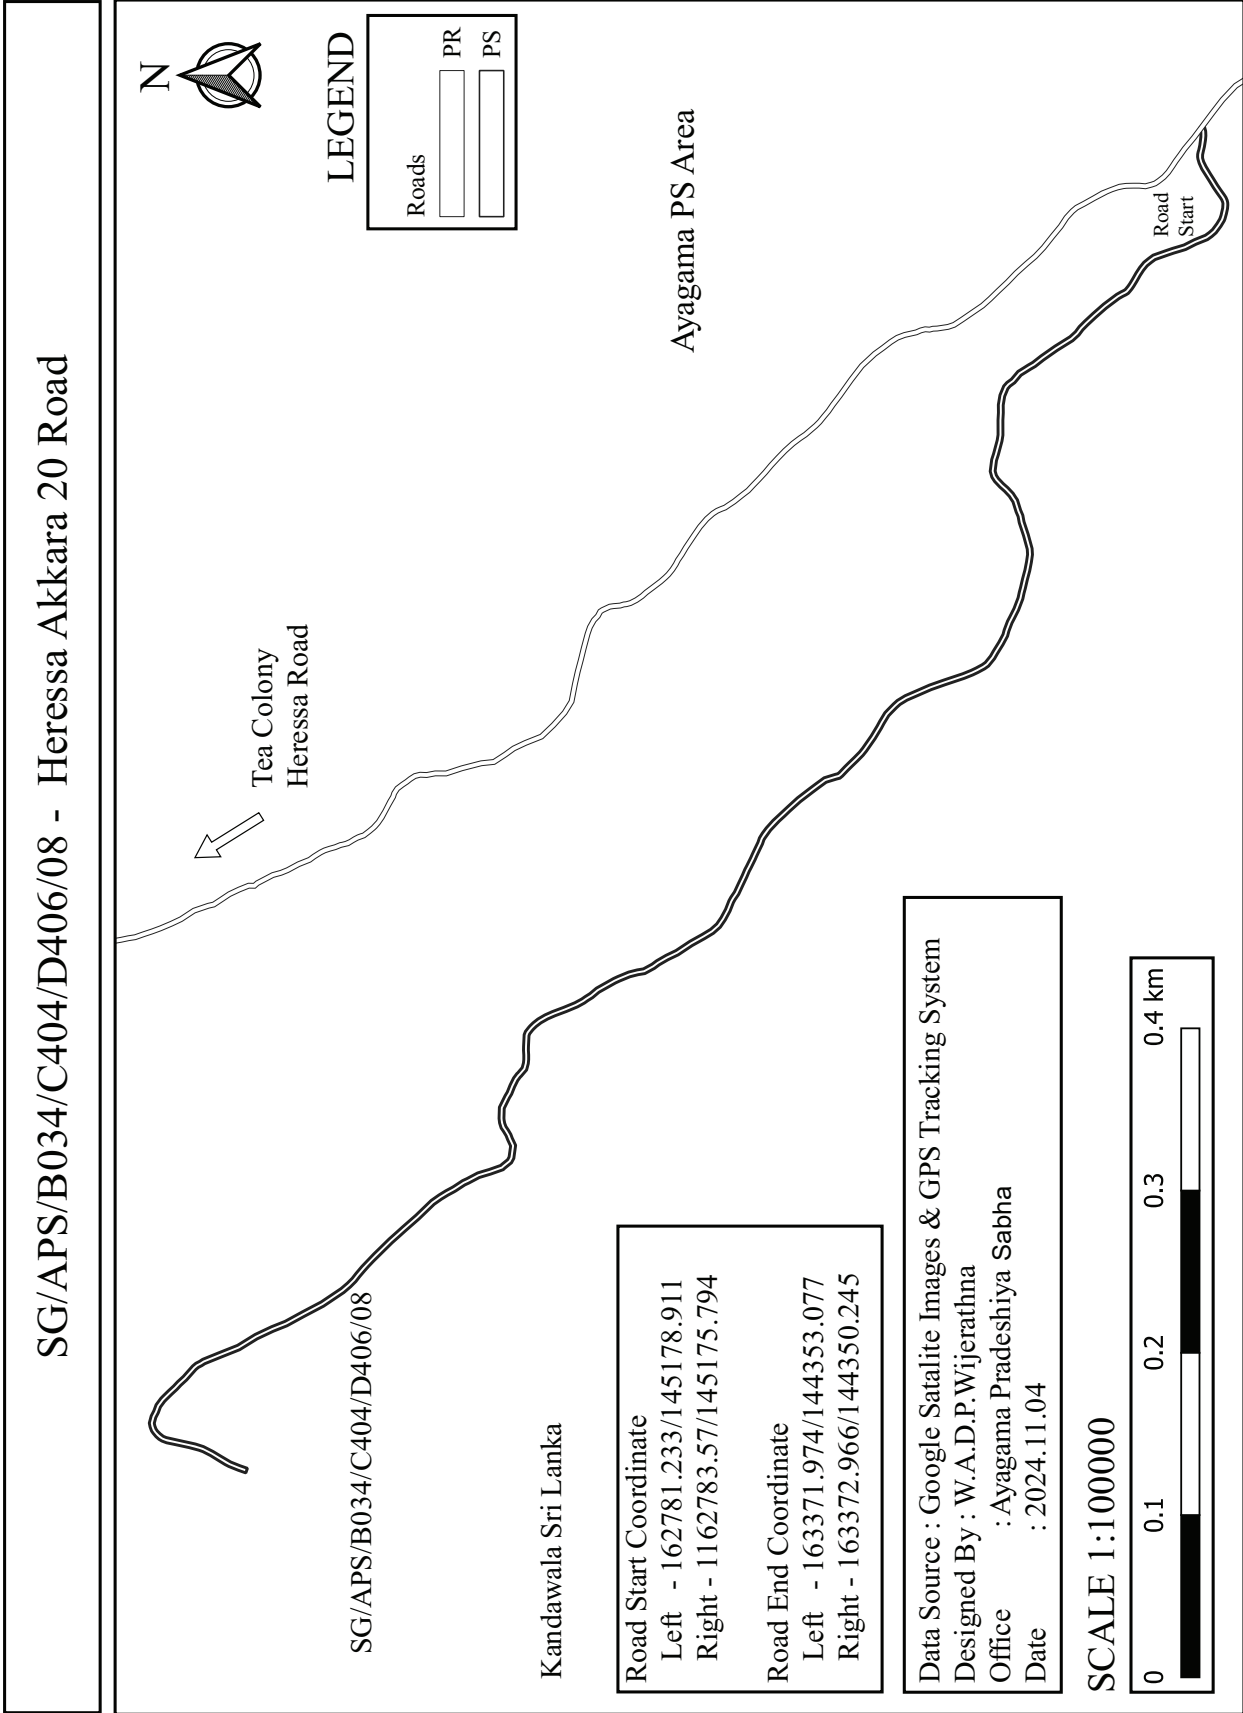


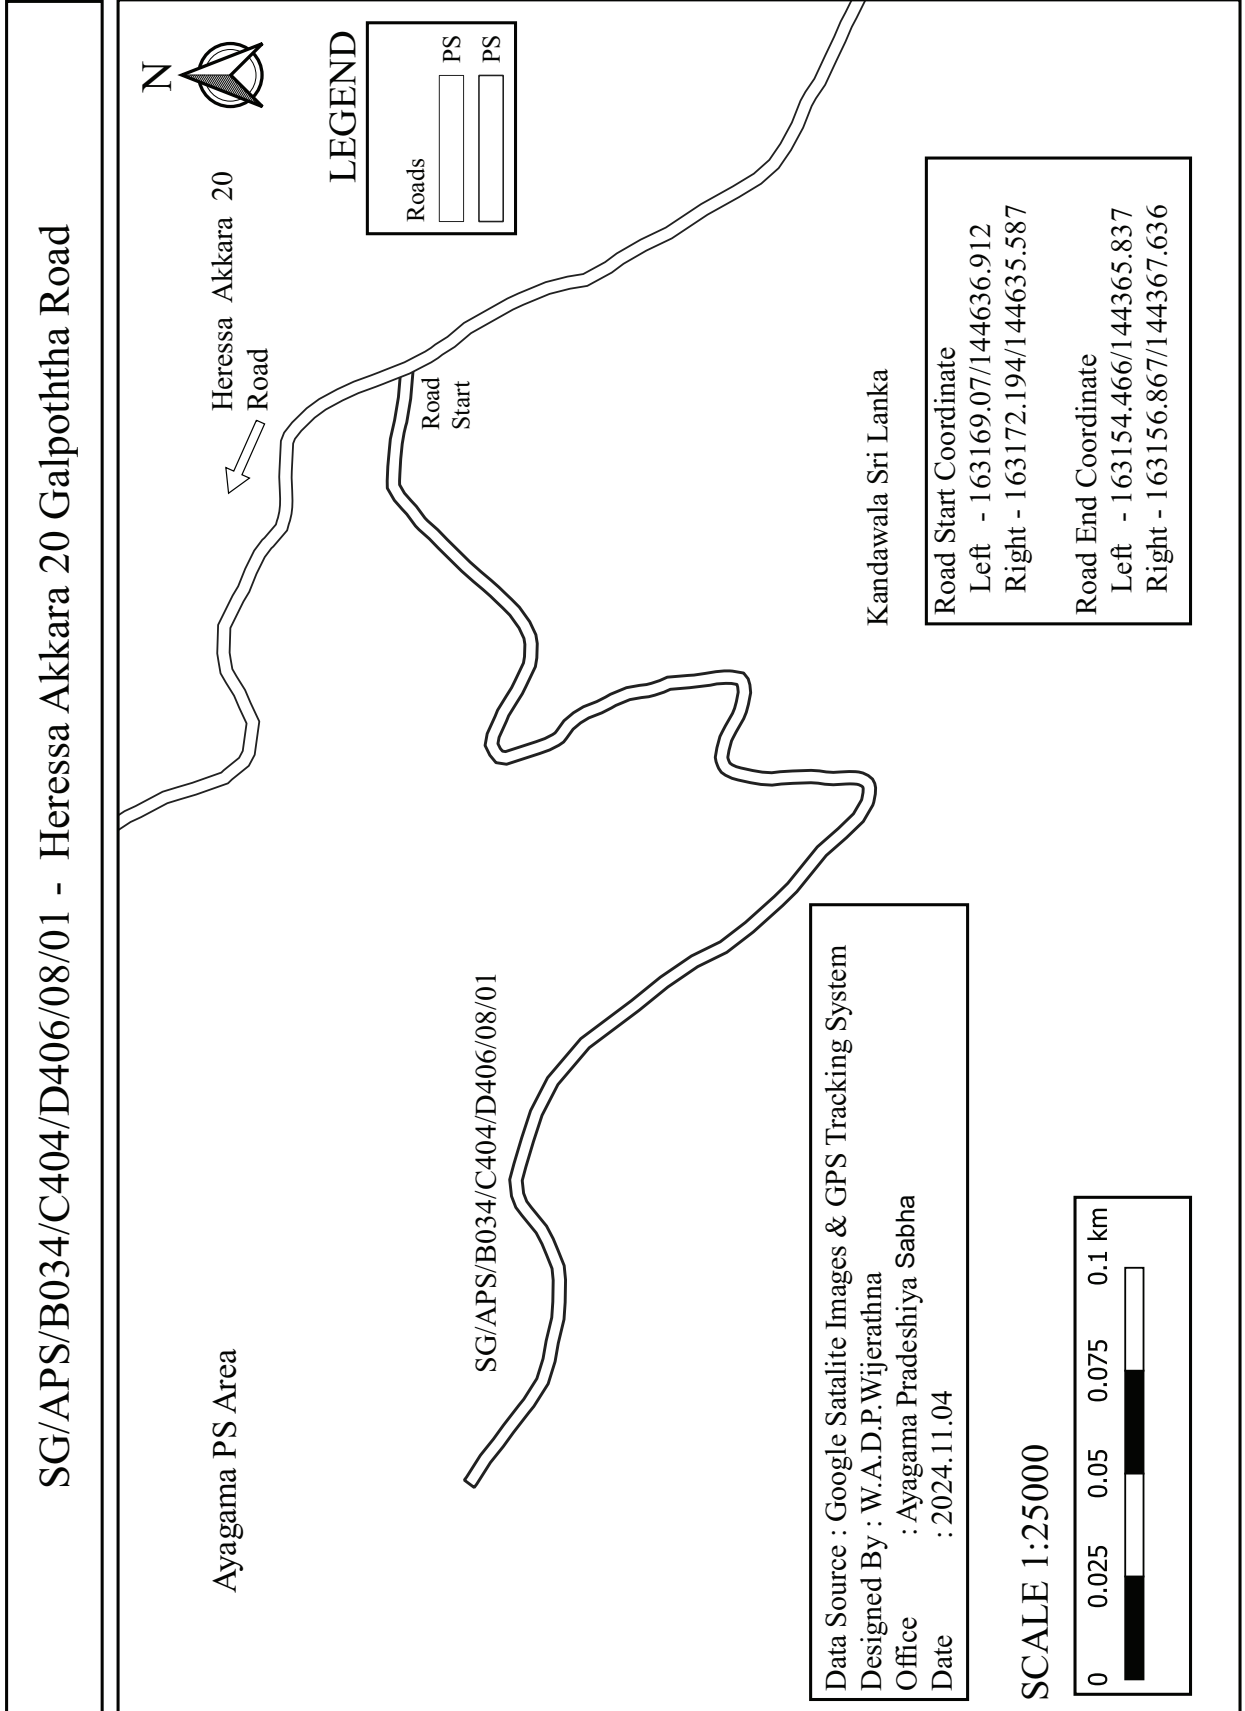


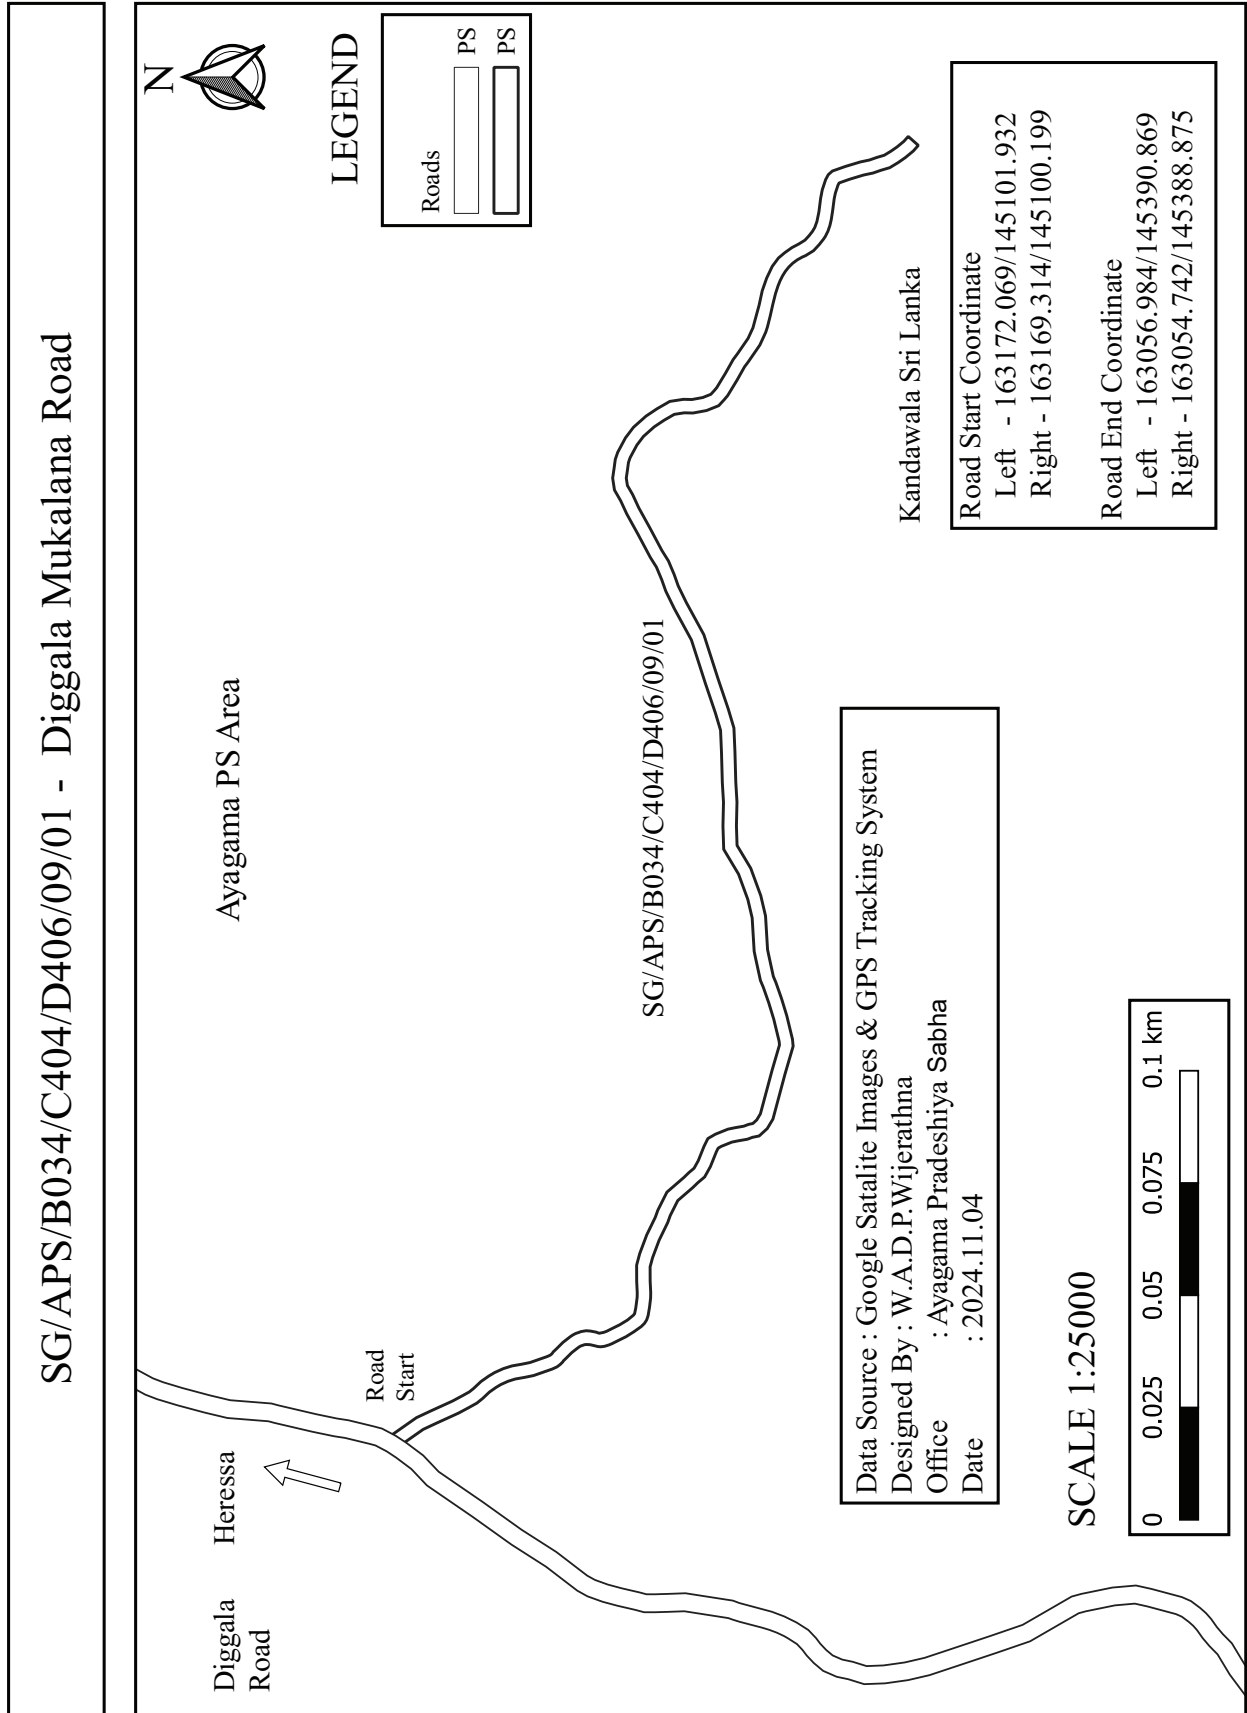


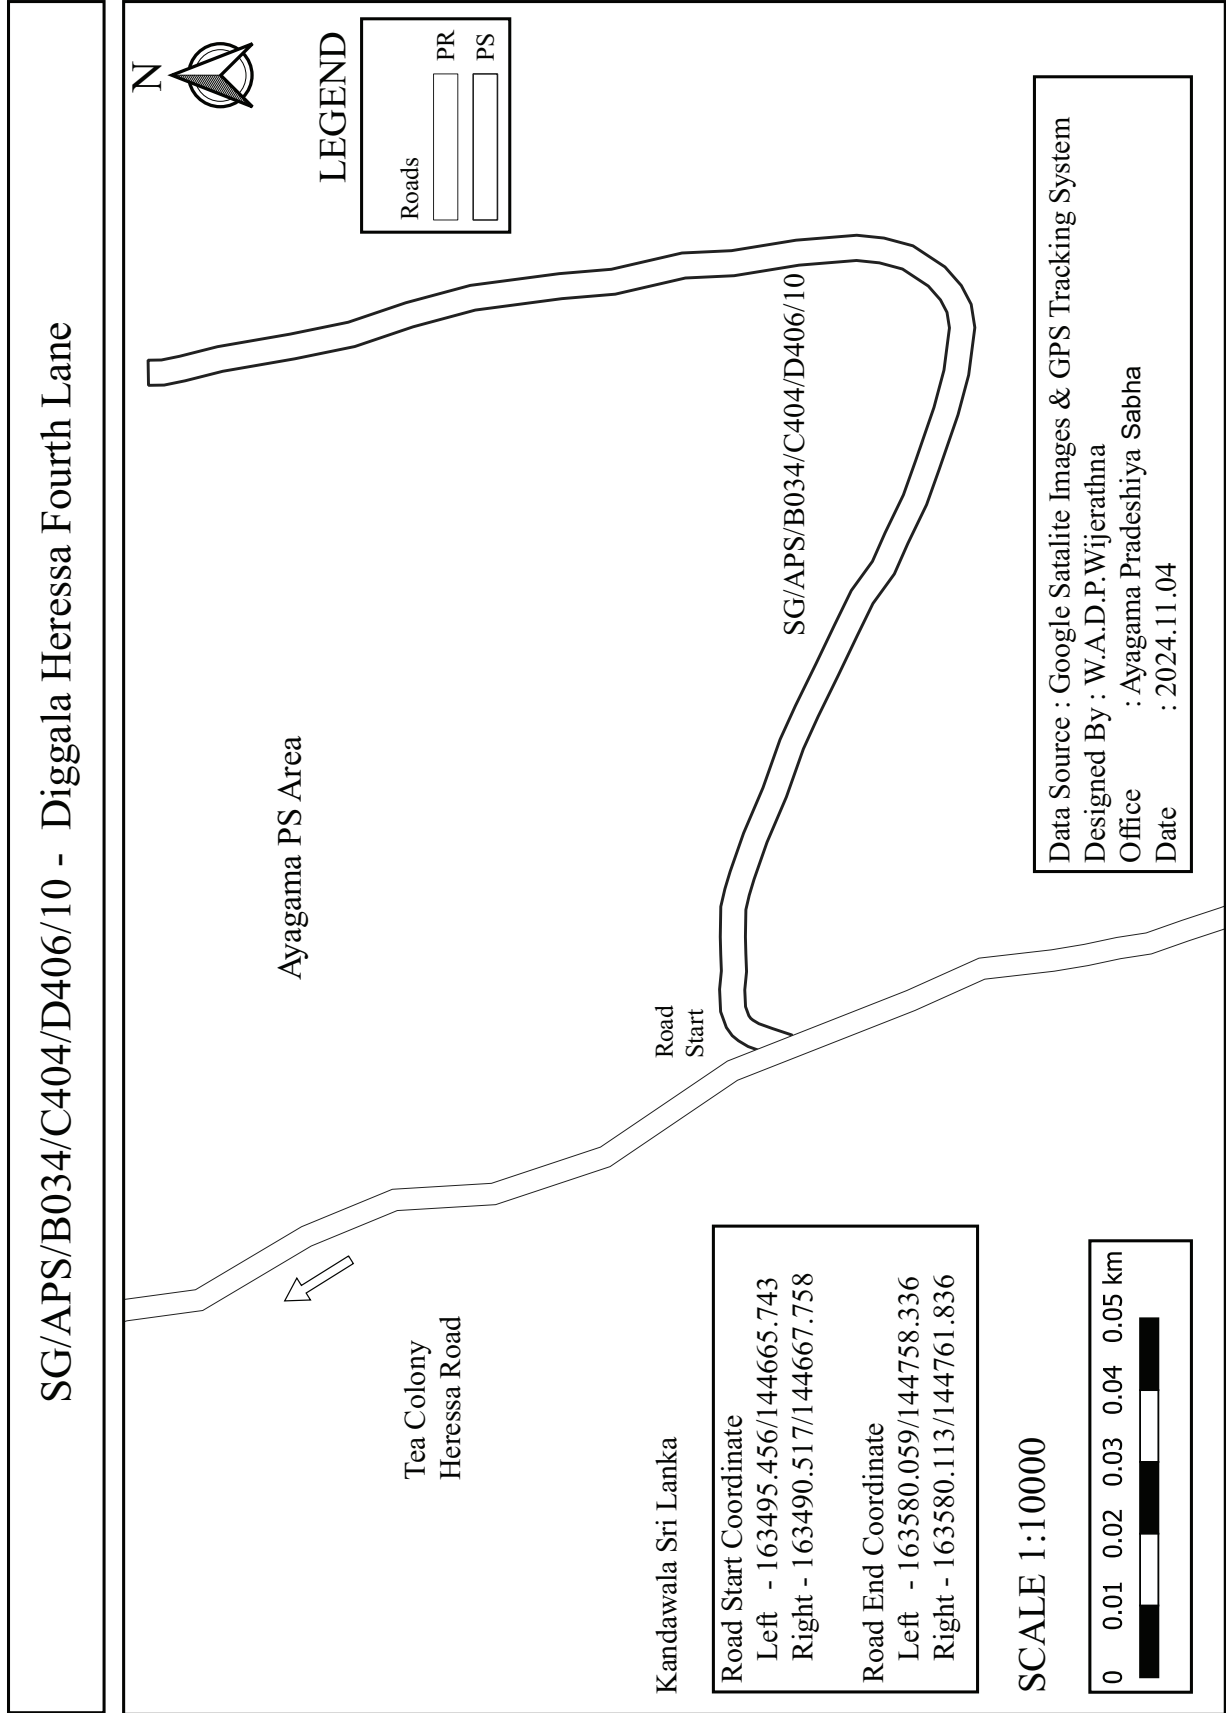


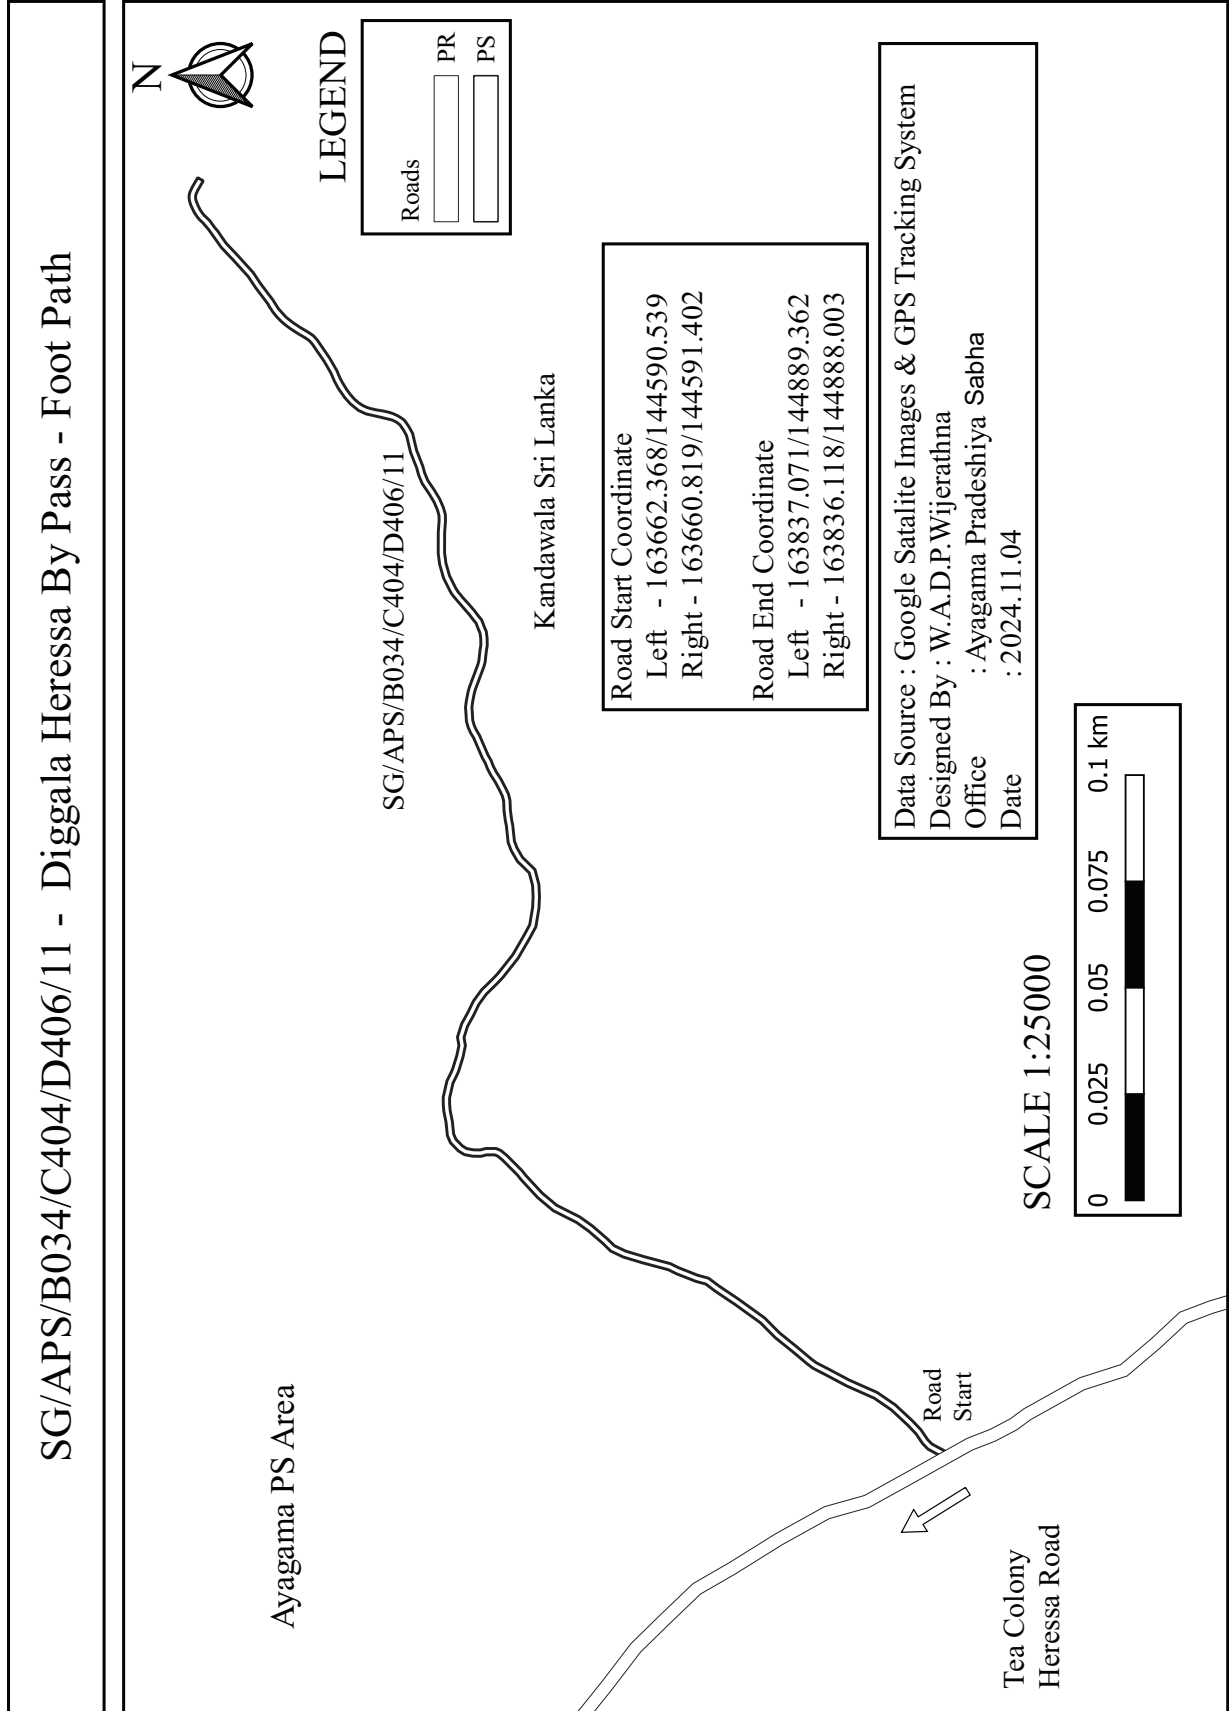


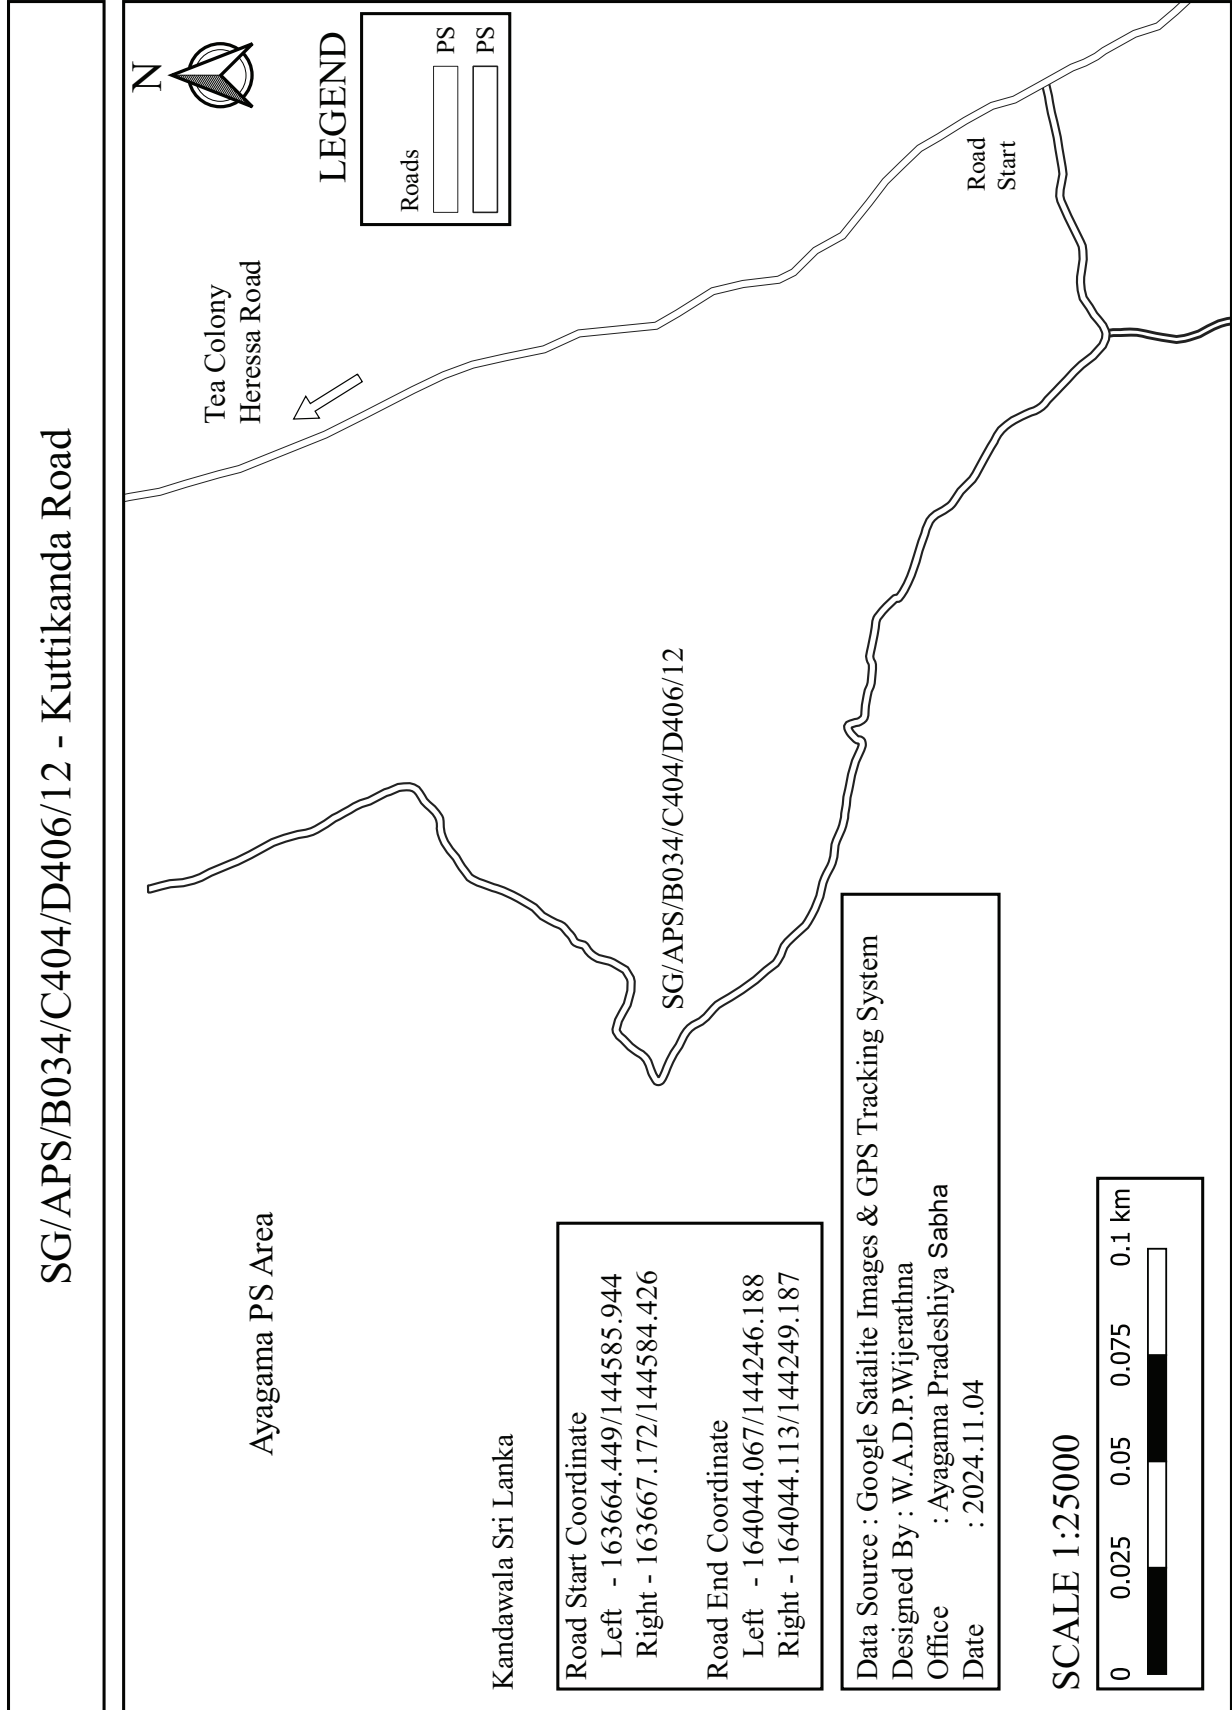

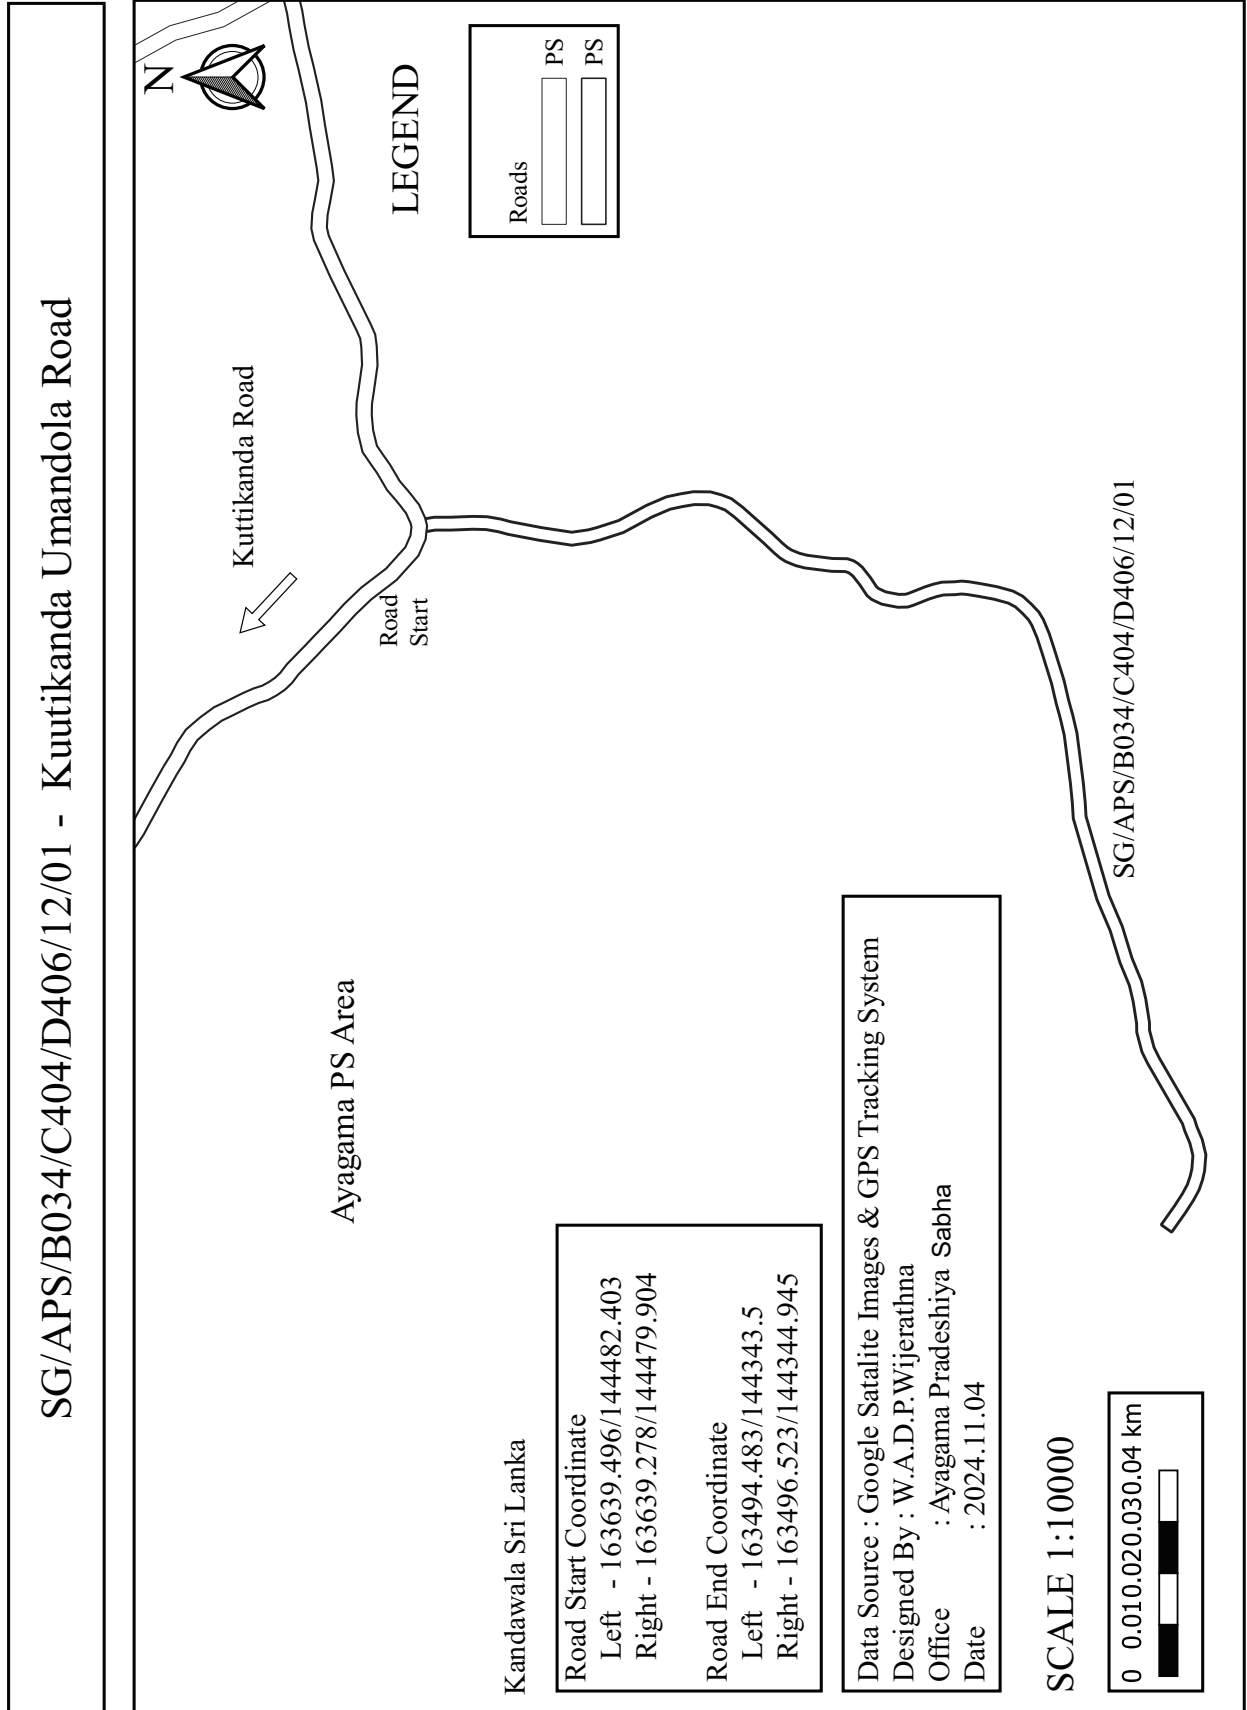

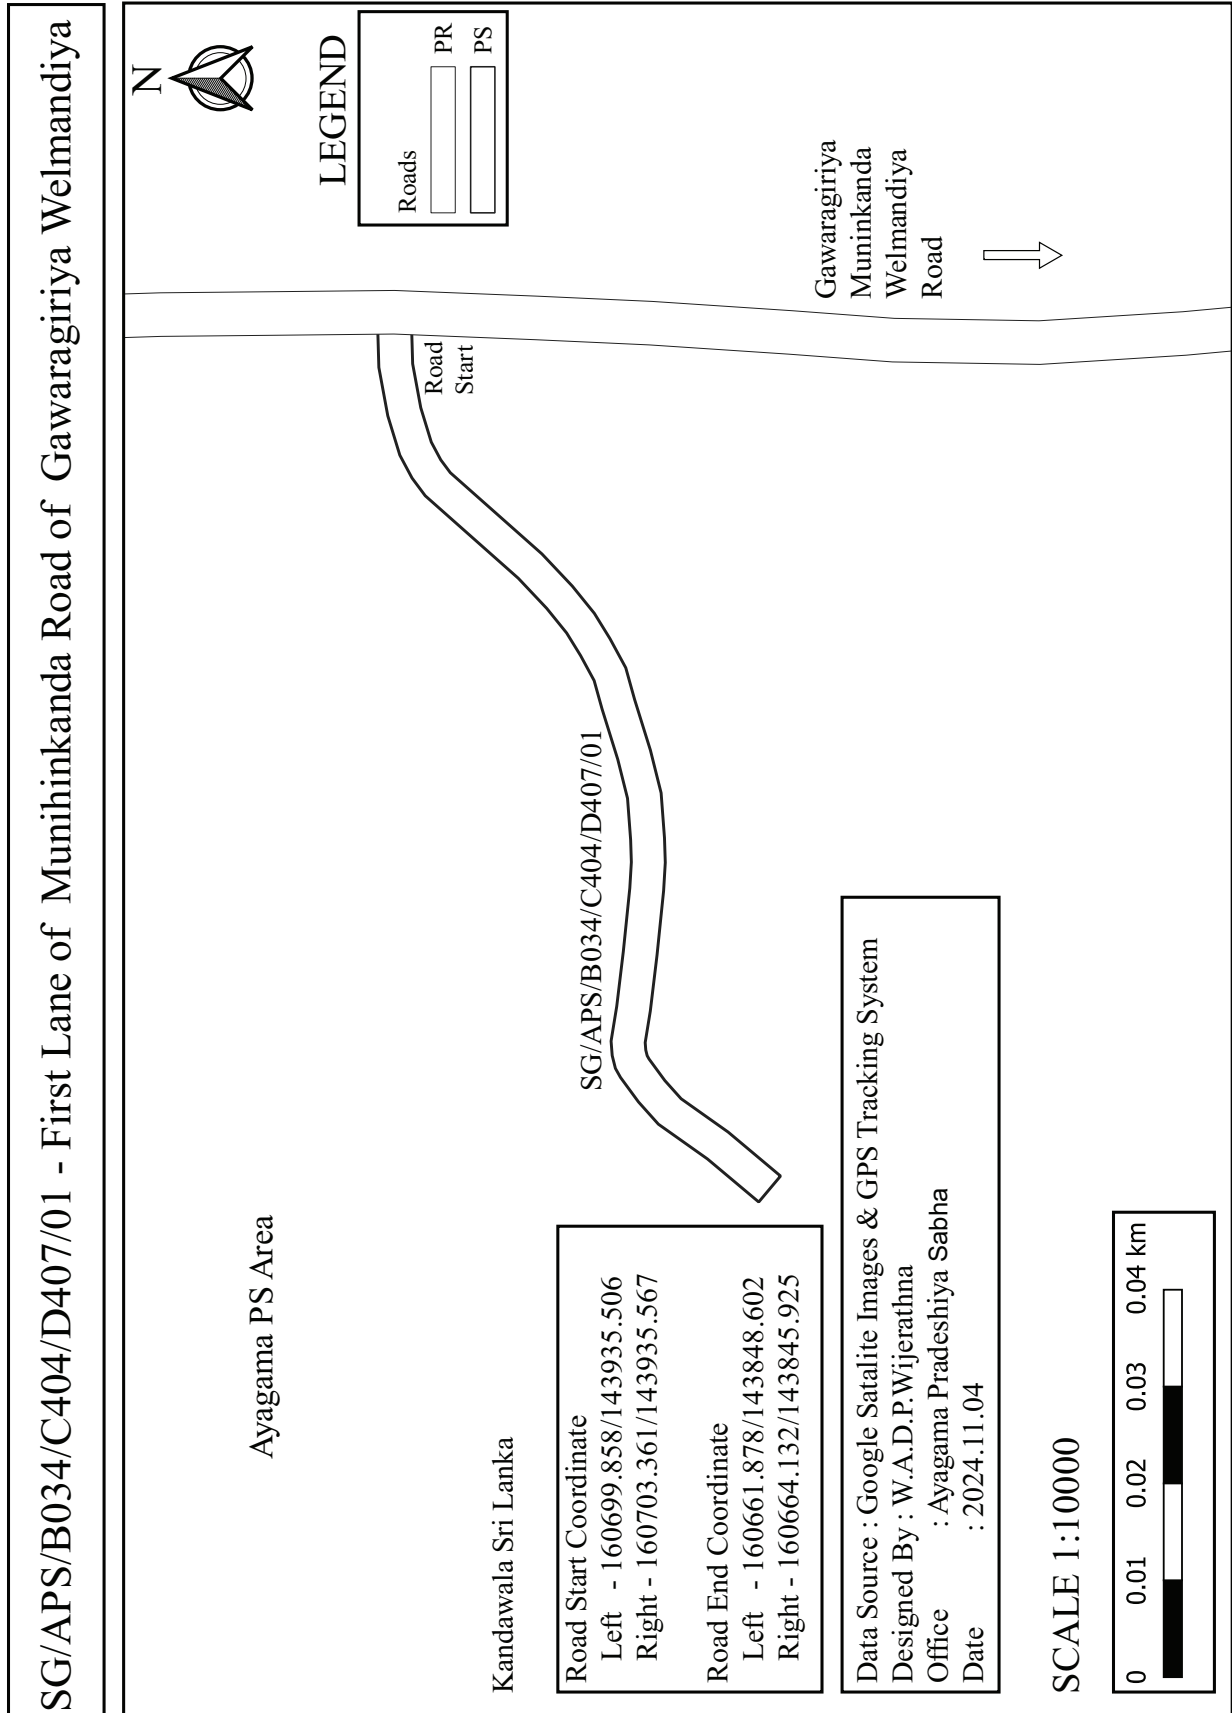

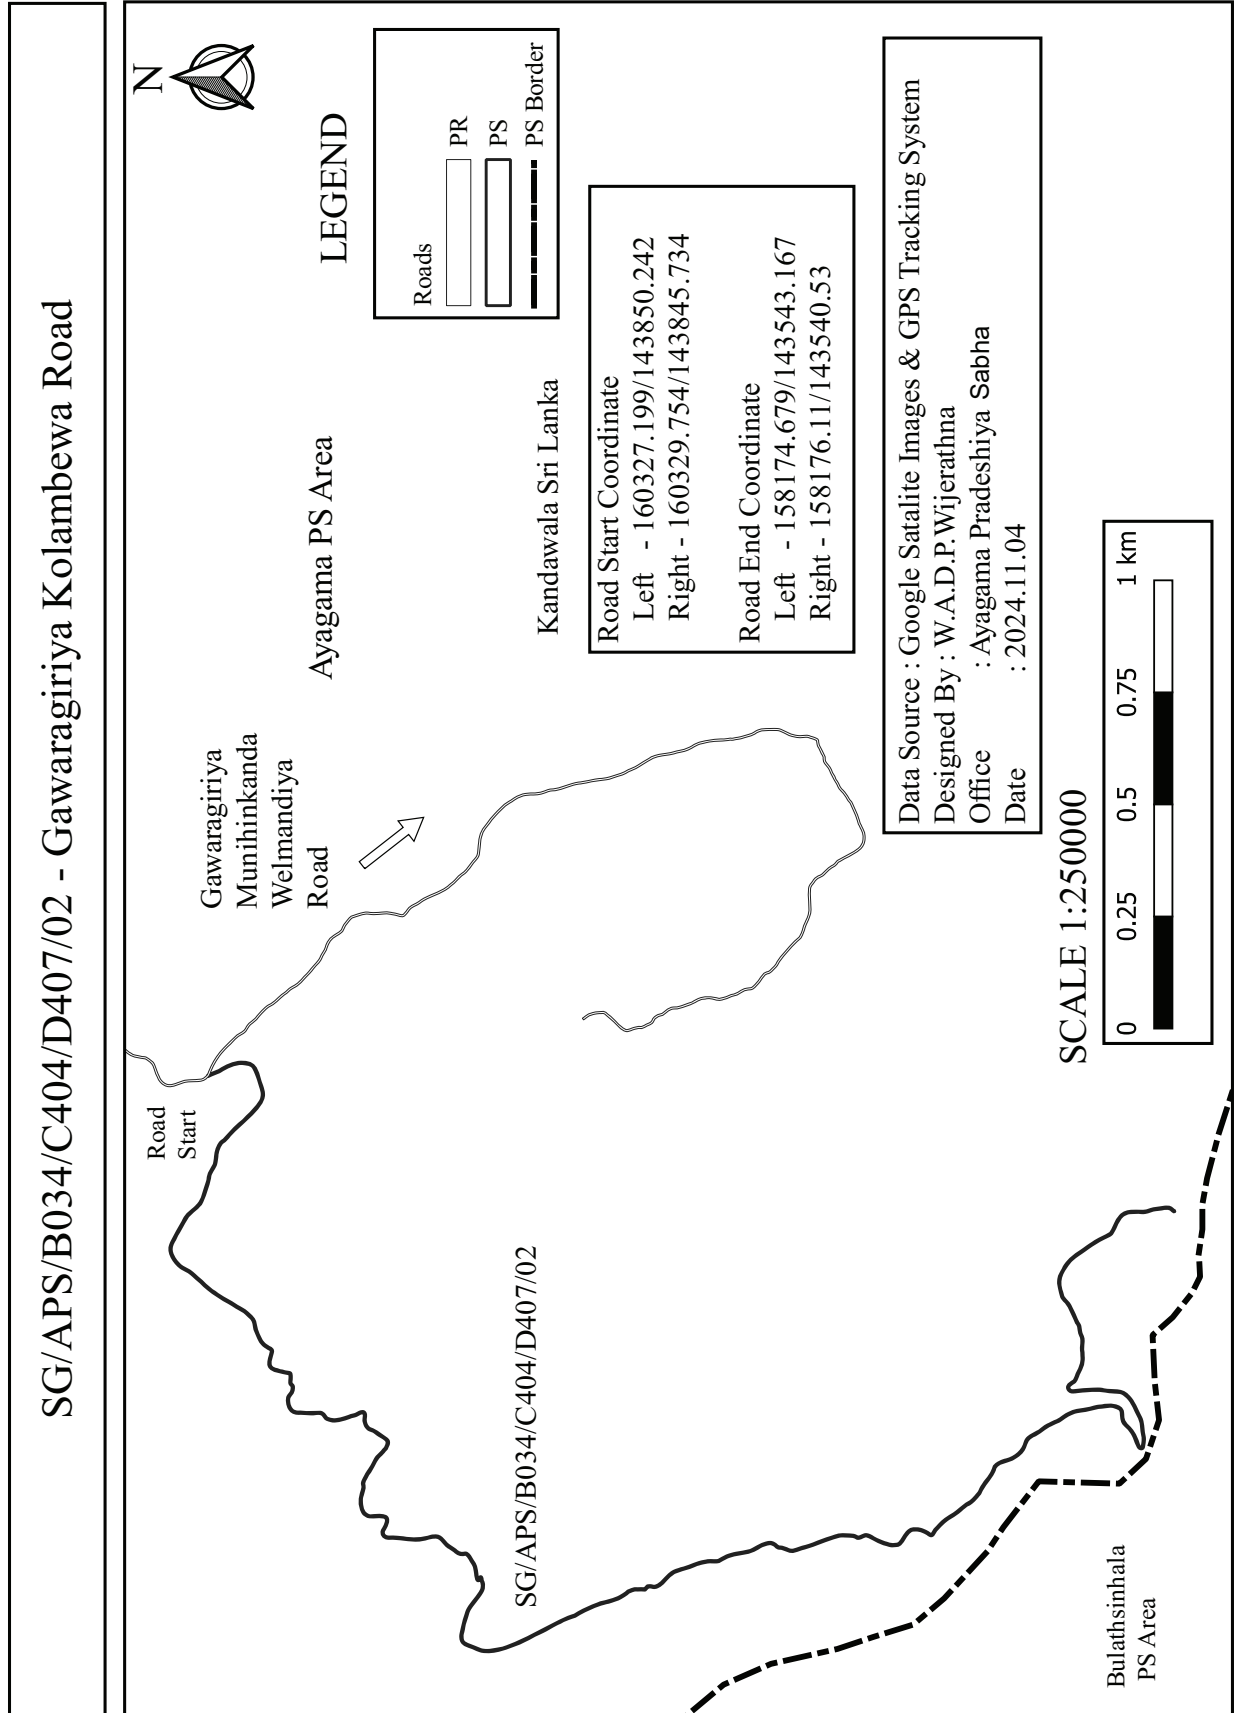

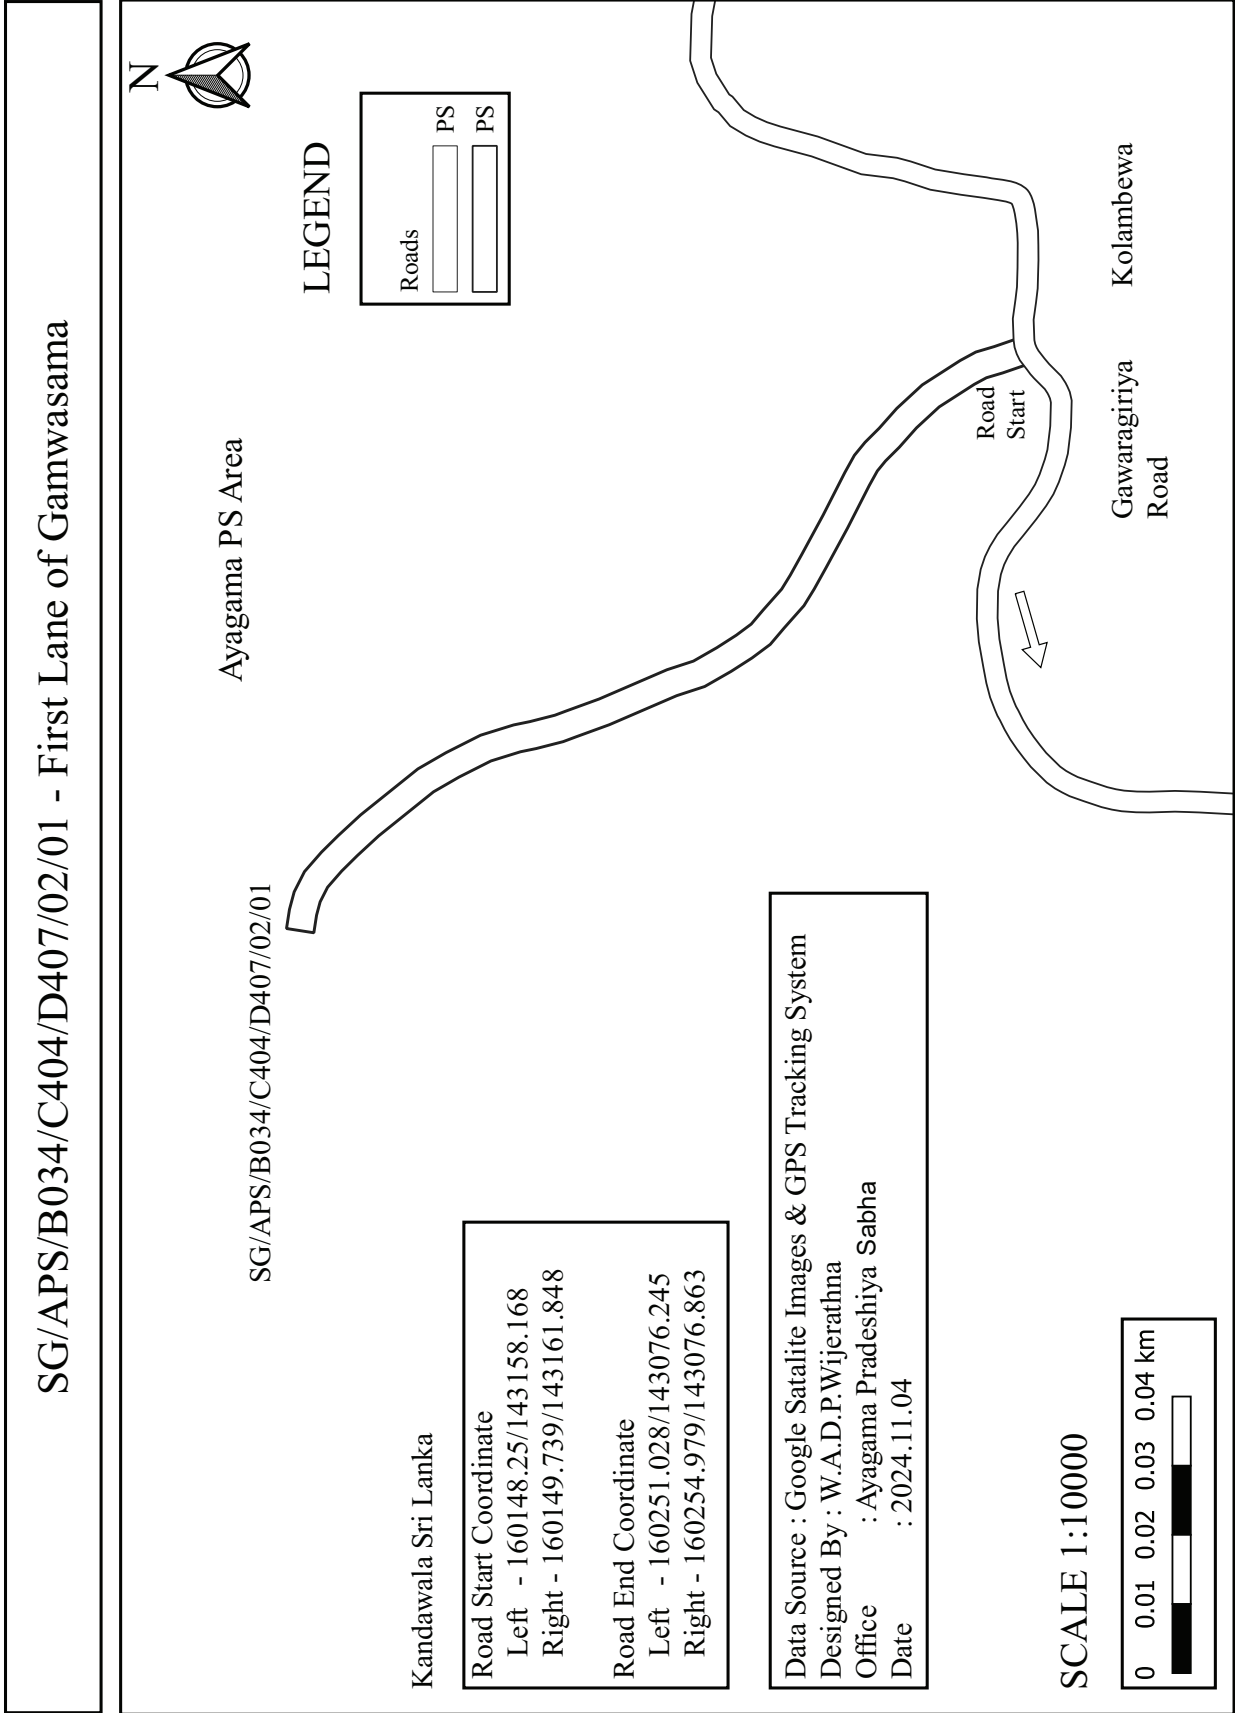

Data Source : Google Satalite Images & GPS Tracking System


Designed By : W.A.D.P.Wijerathna


Office : Ayagama Pradeshiya Sabha


Date : 2024.11.04


SCALE 1:10000


0 0.01 0.02 0.03 0.04 km

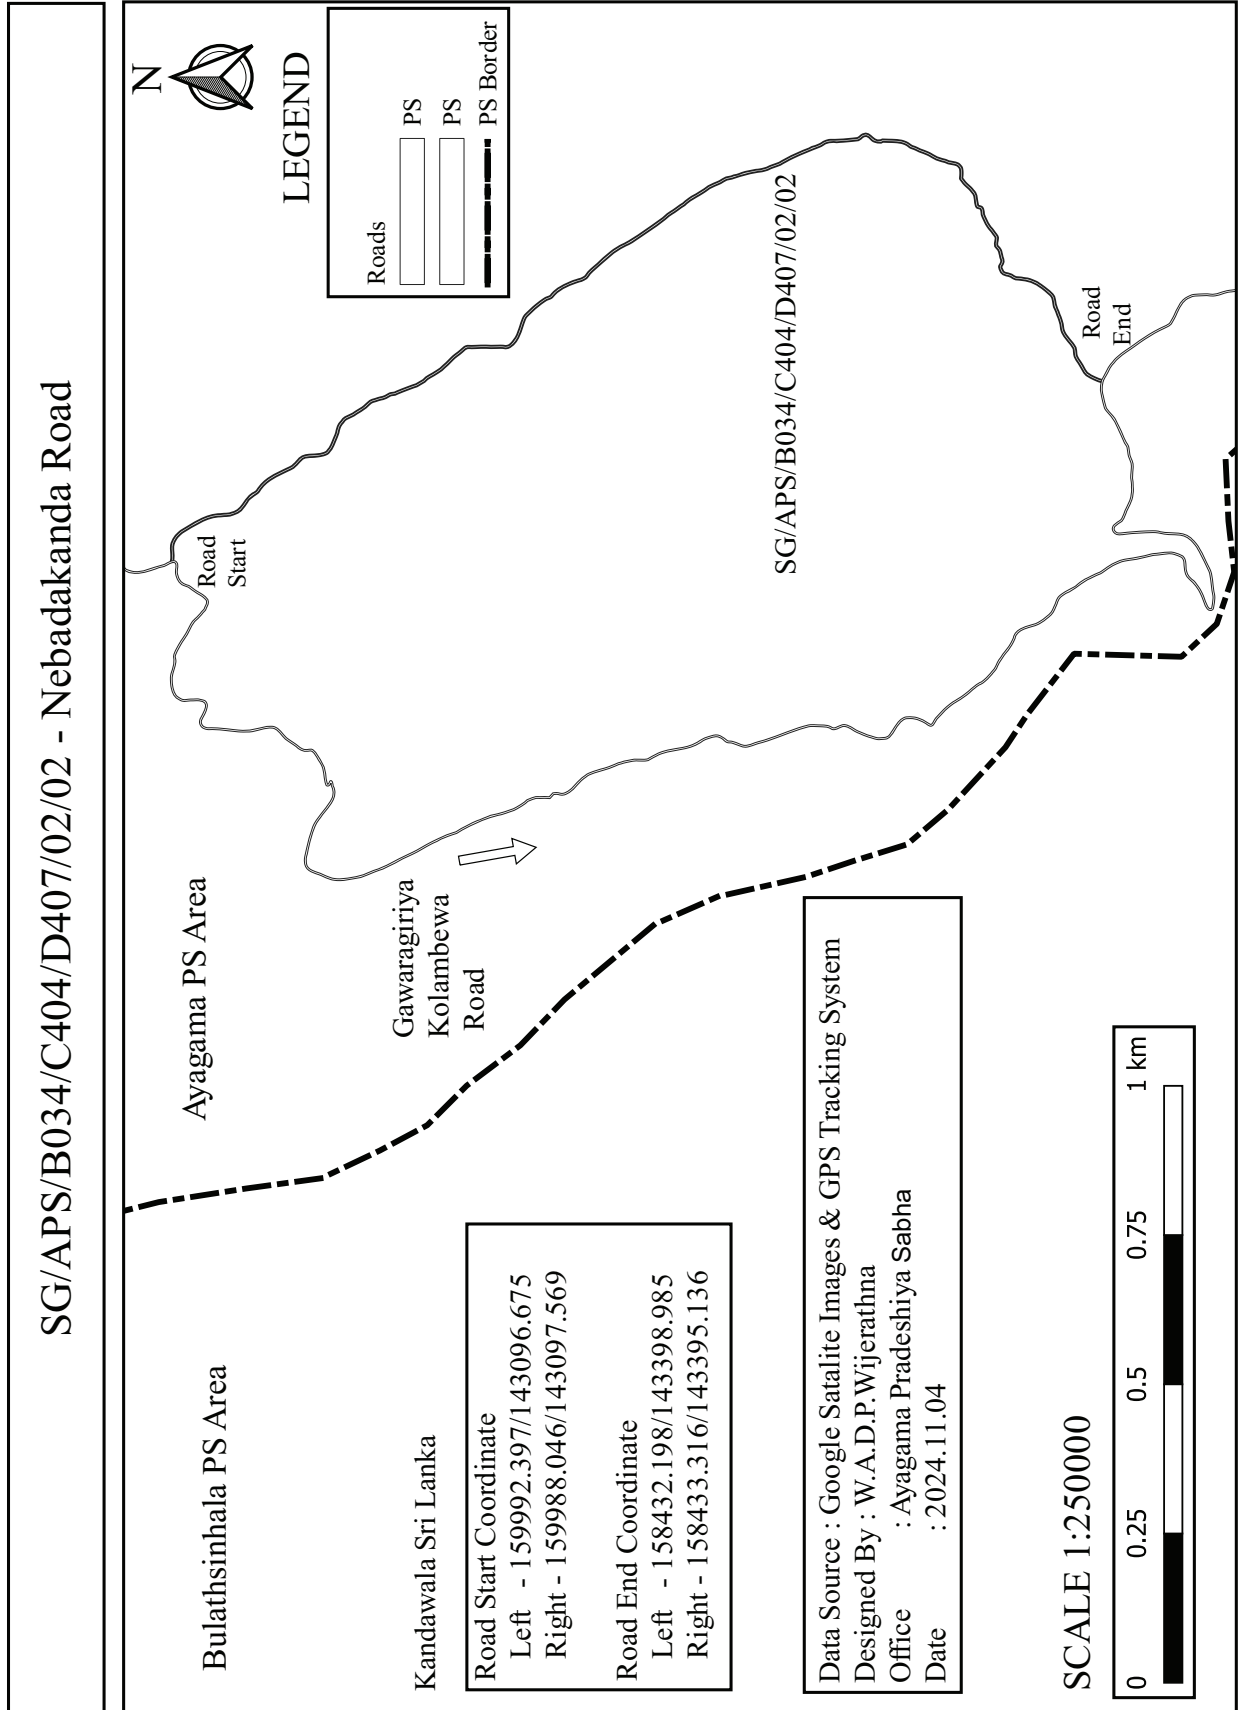


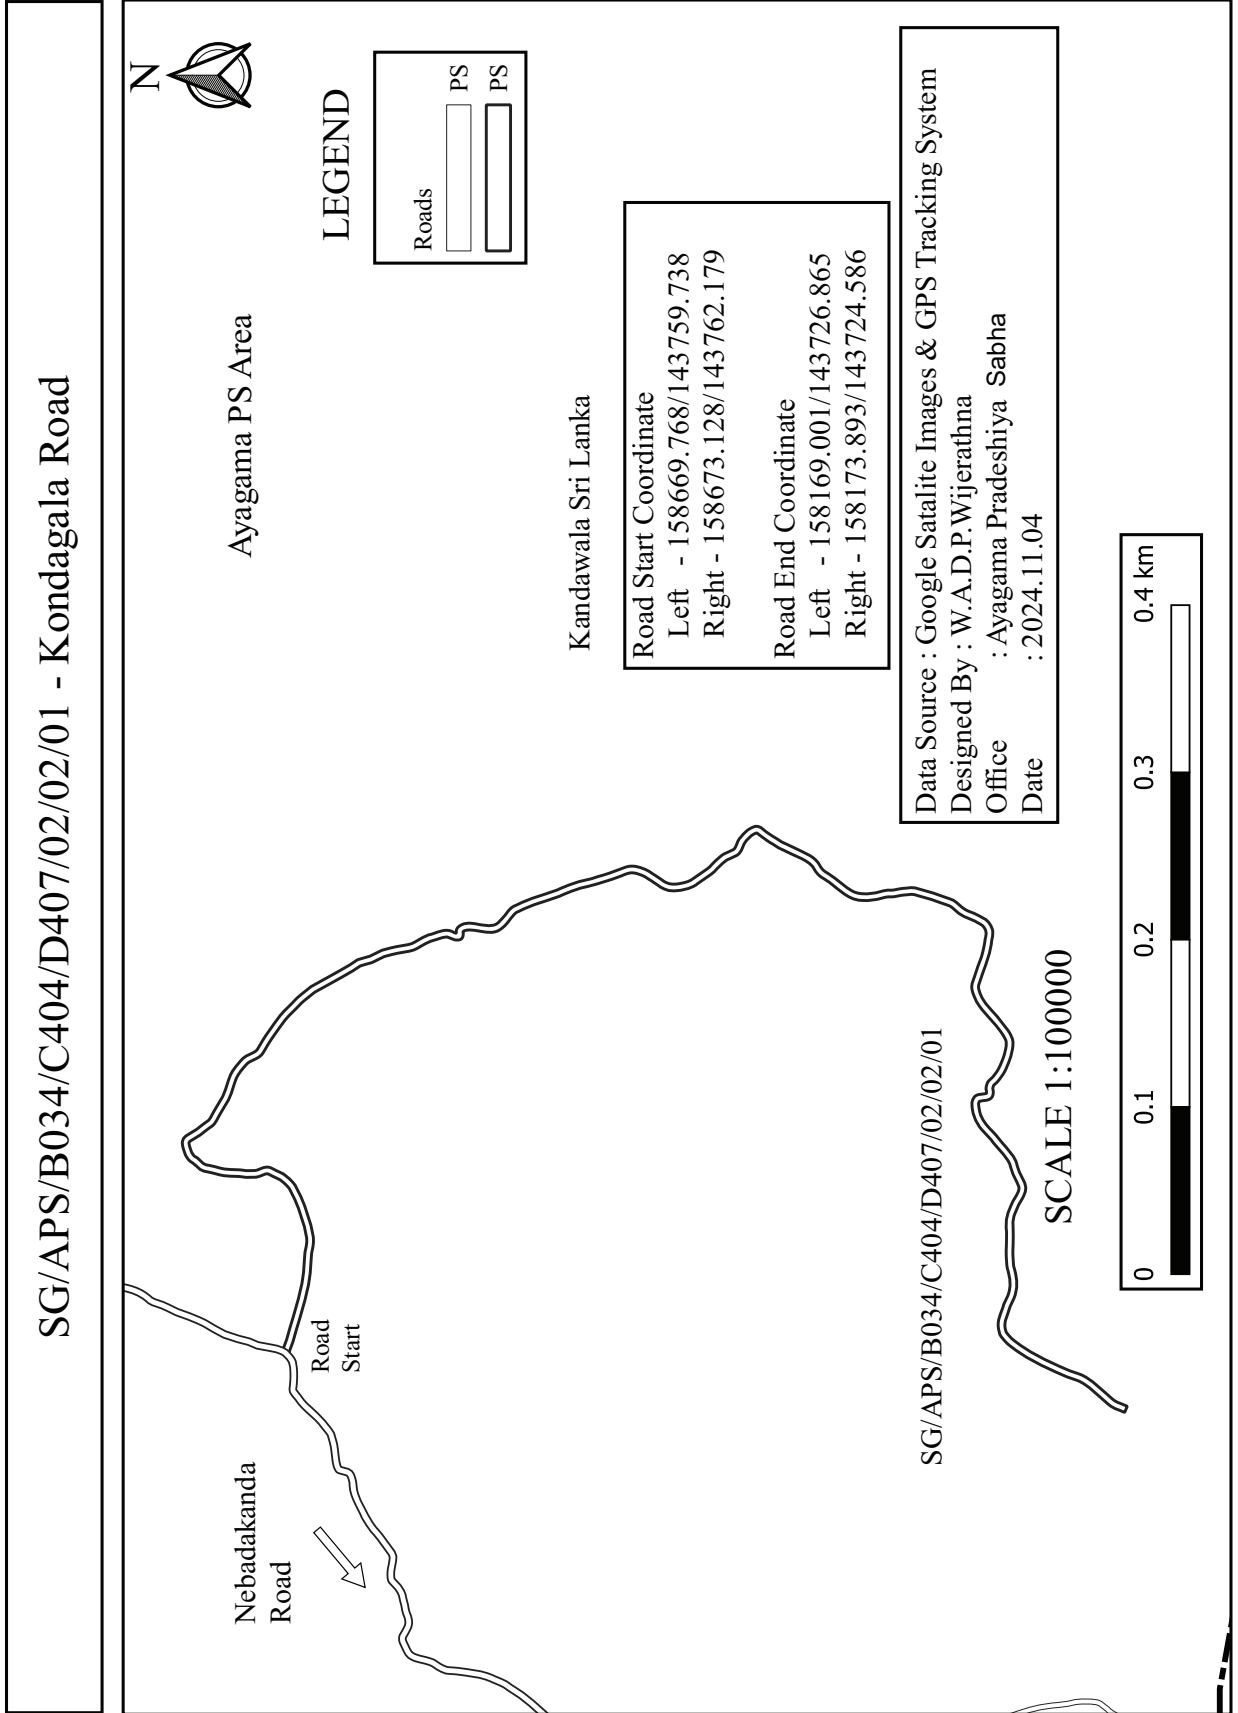


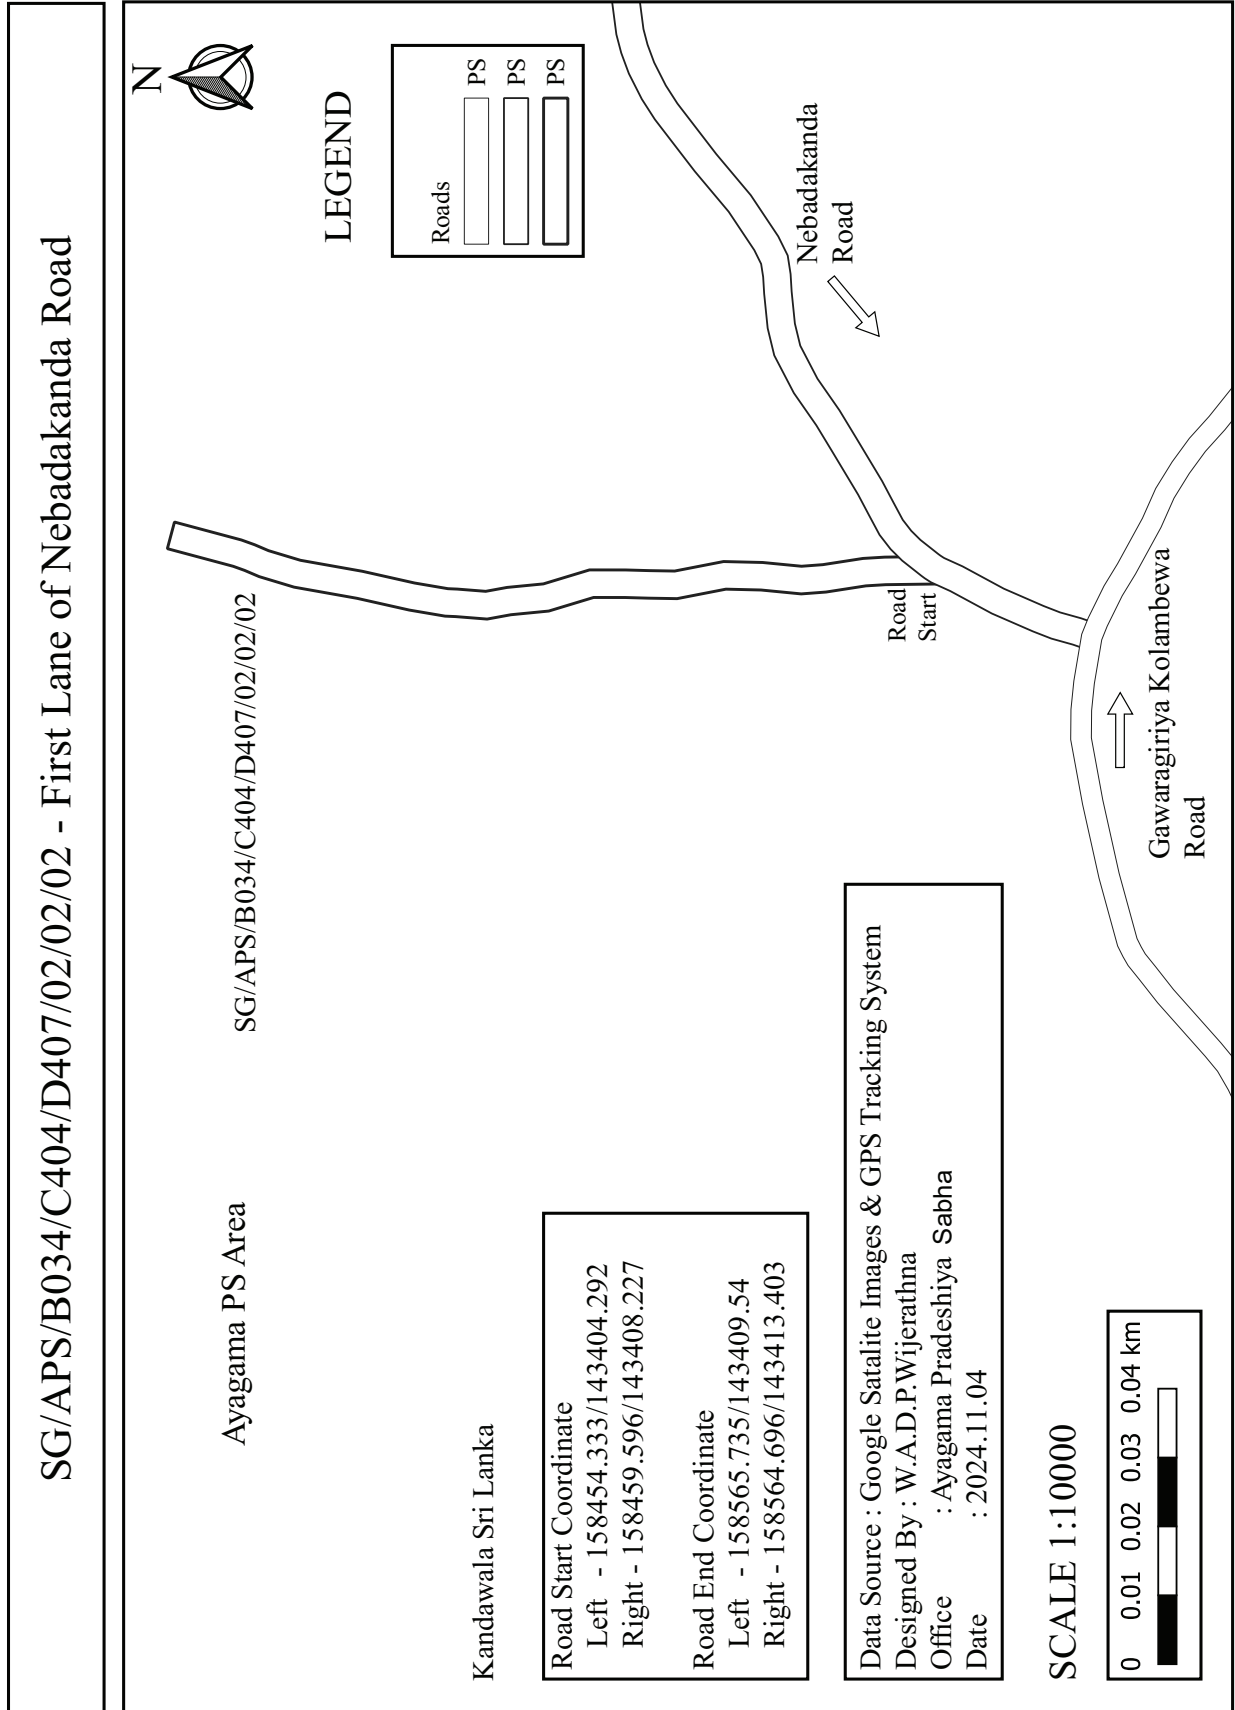


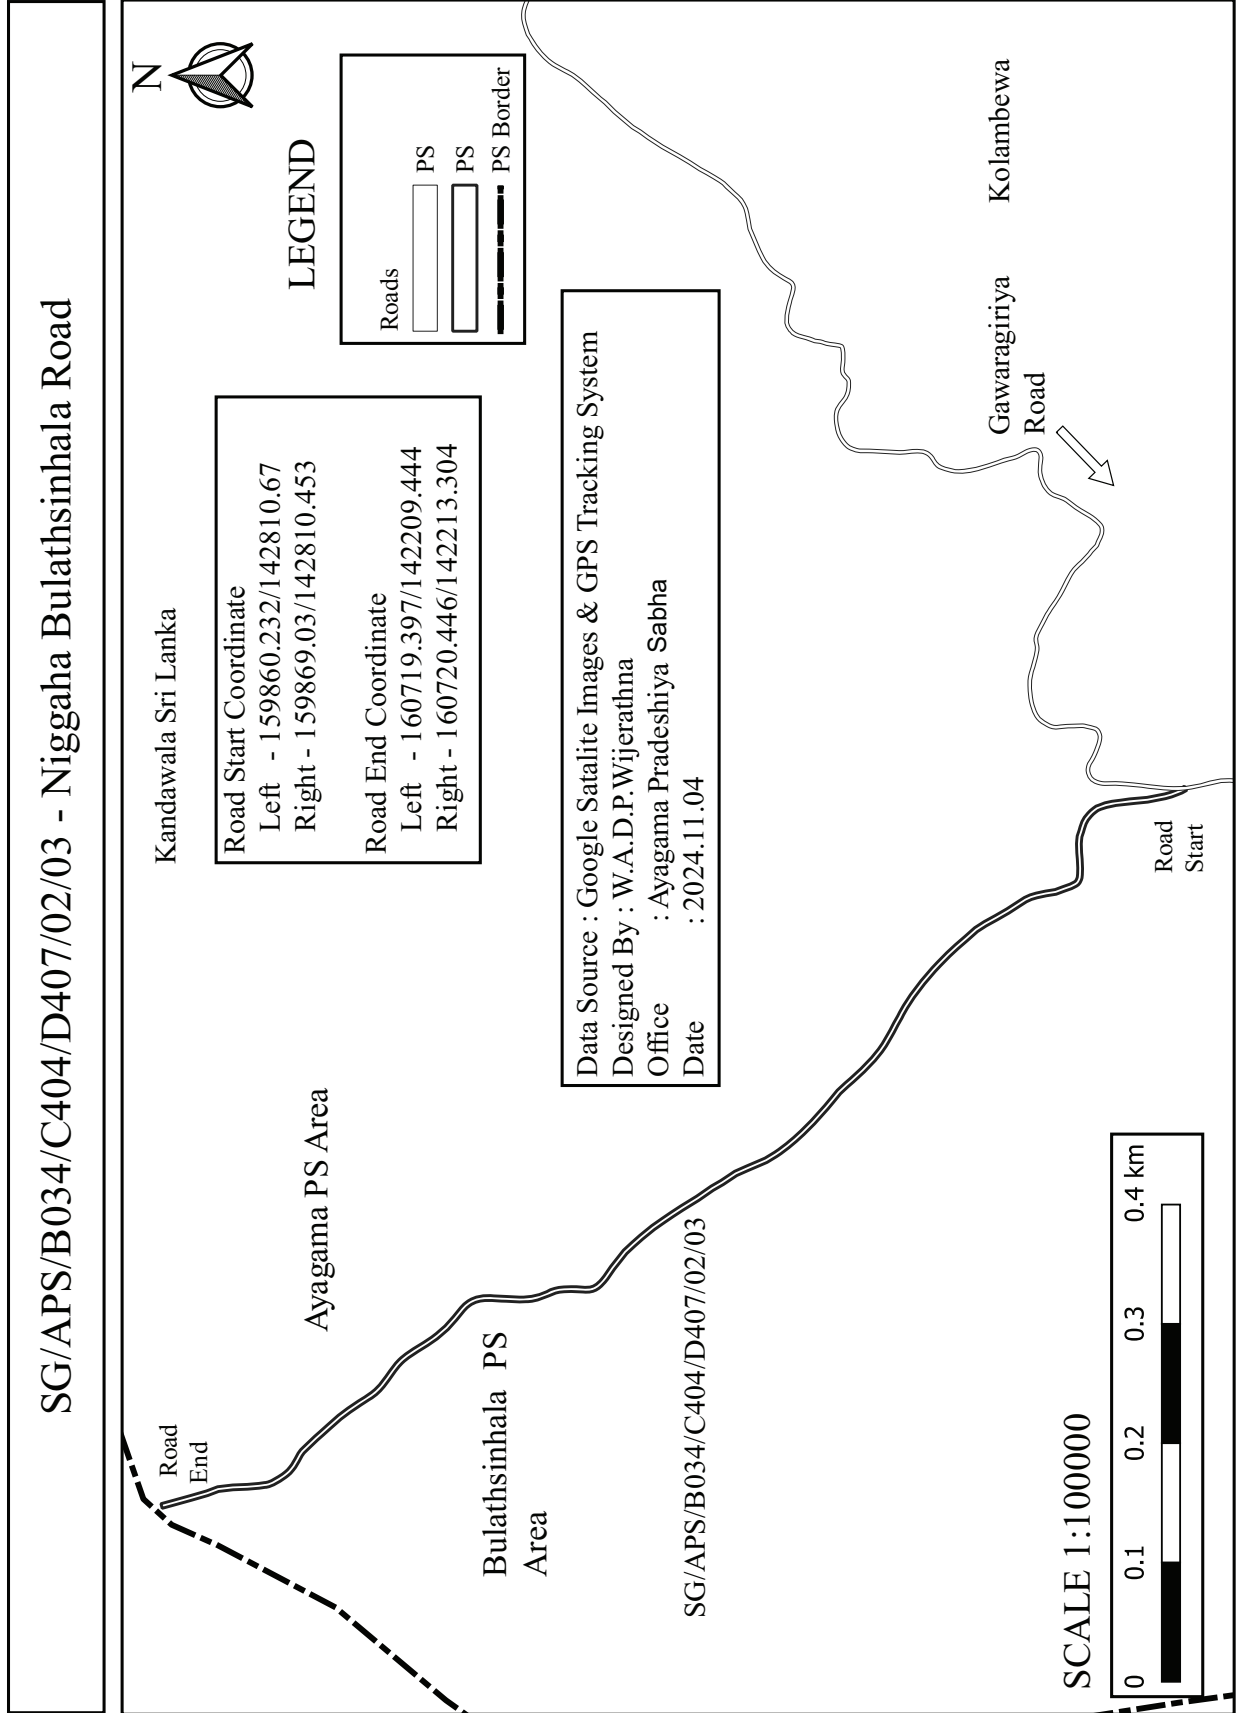


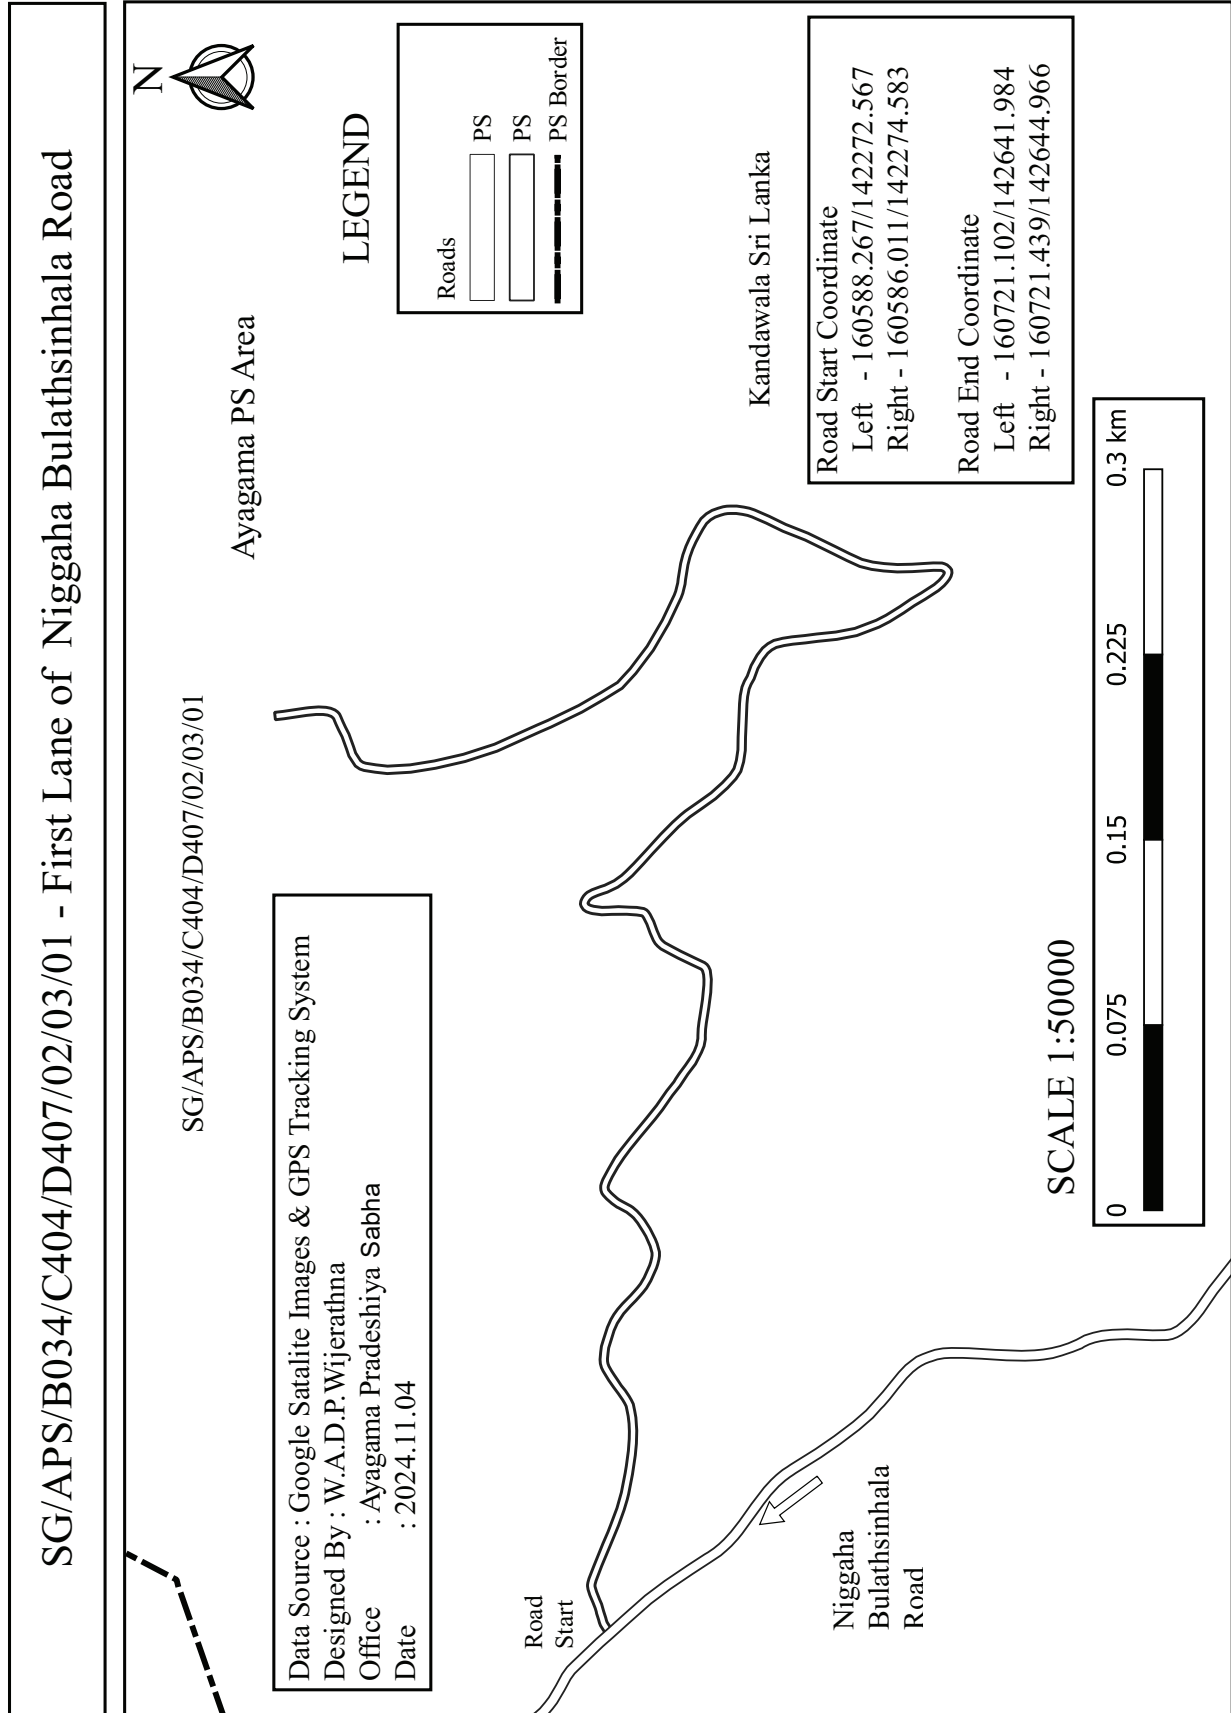


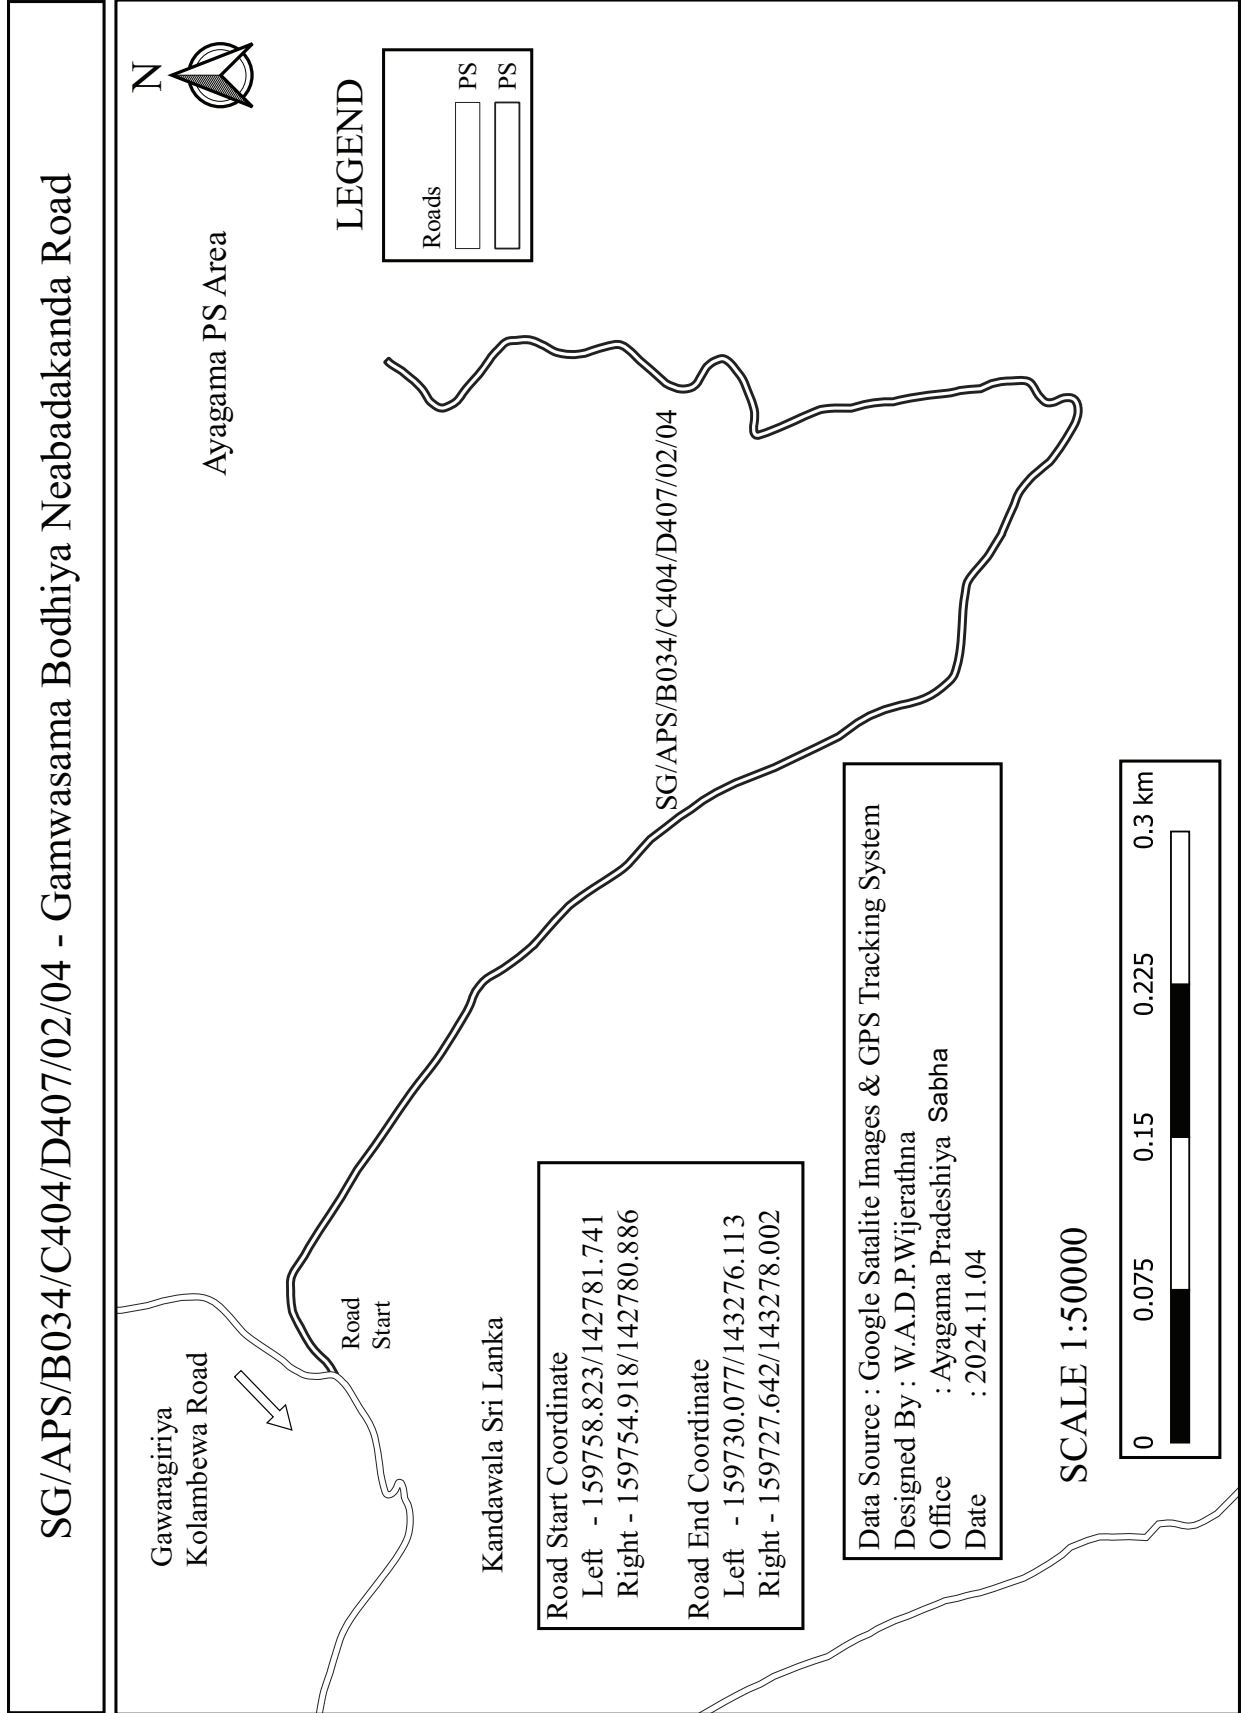


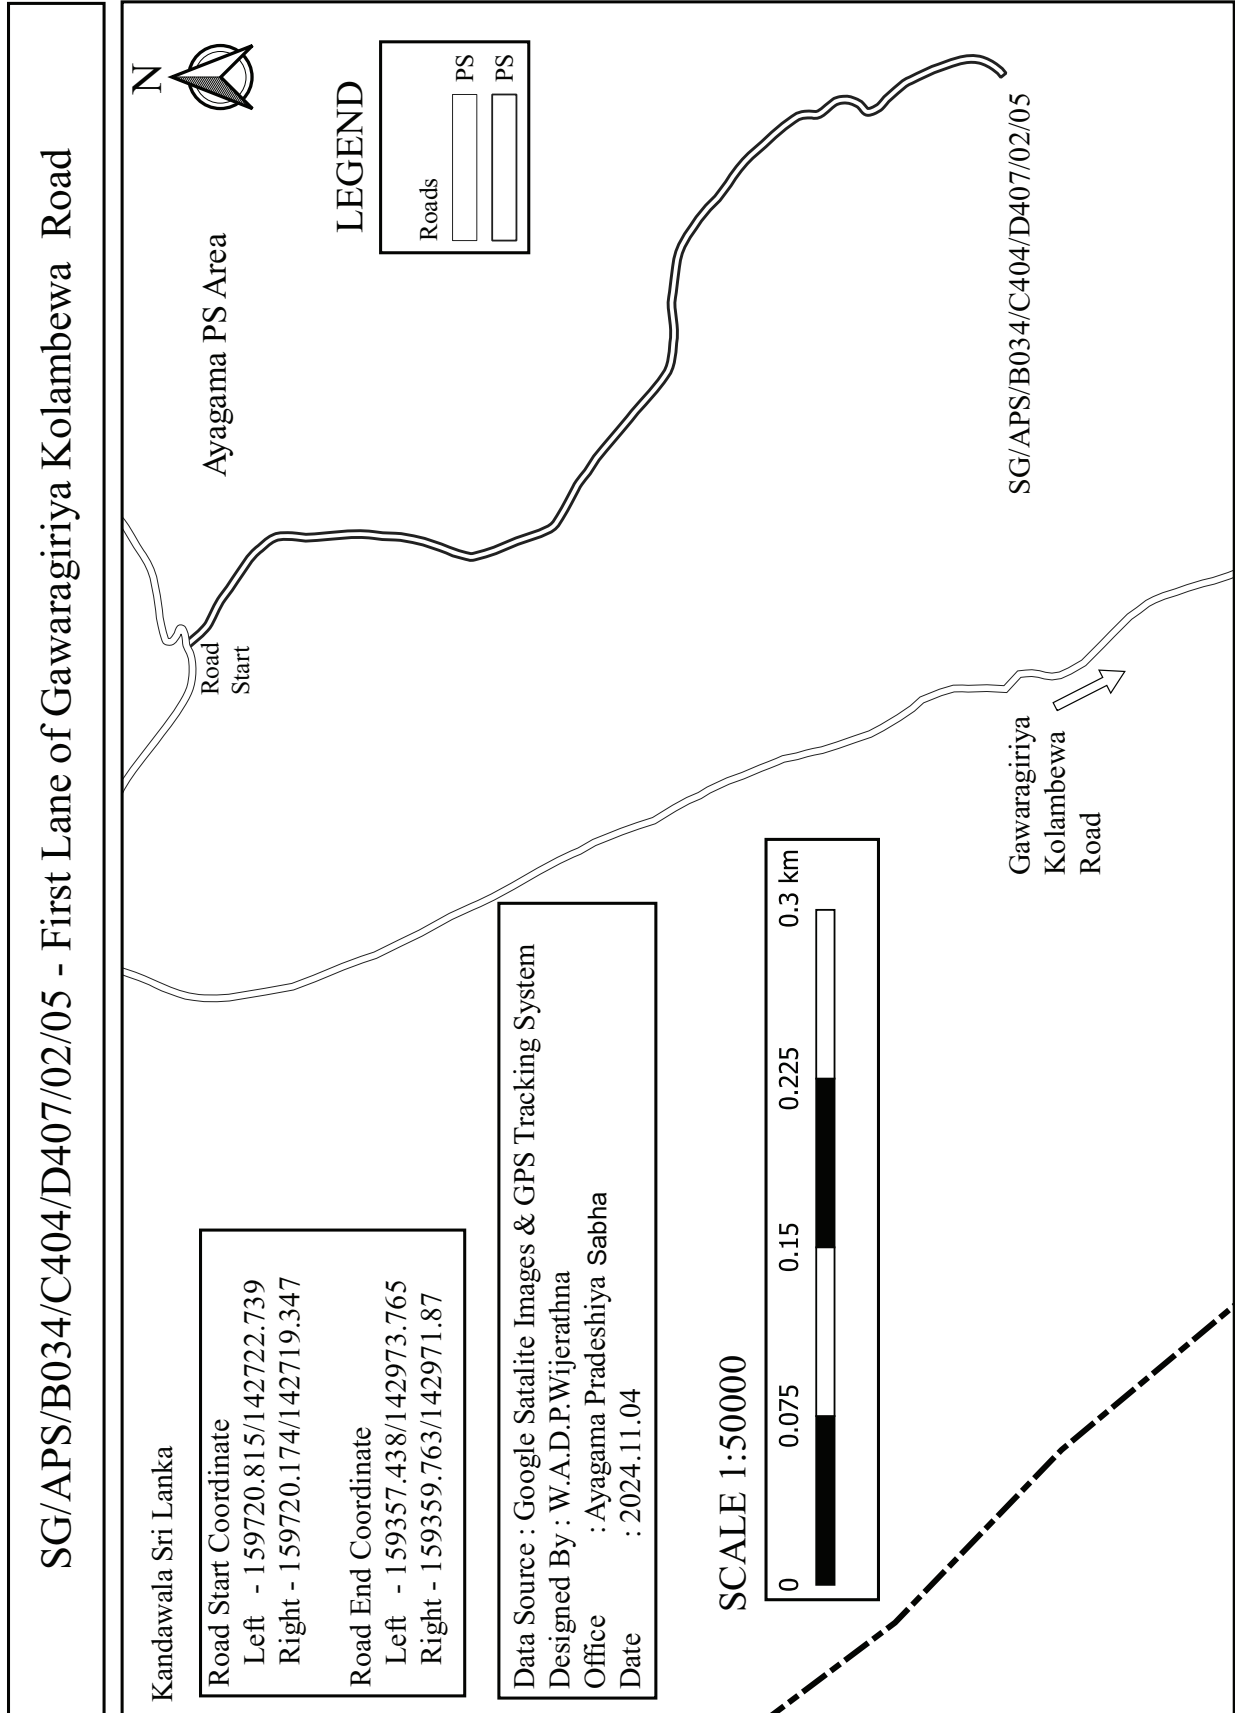


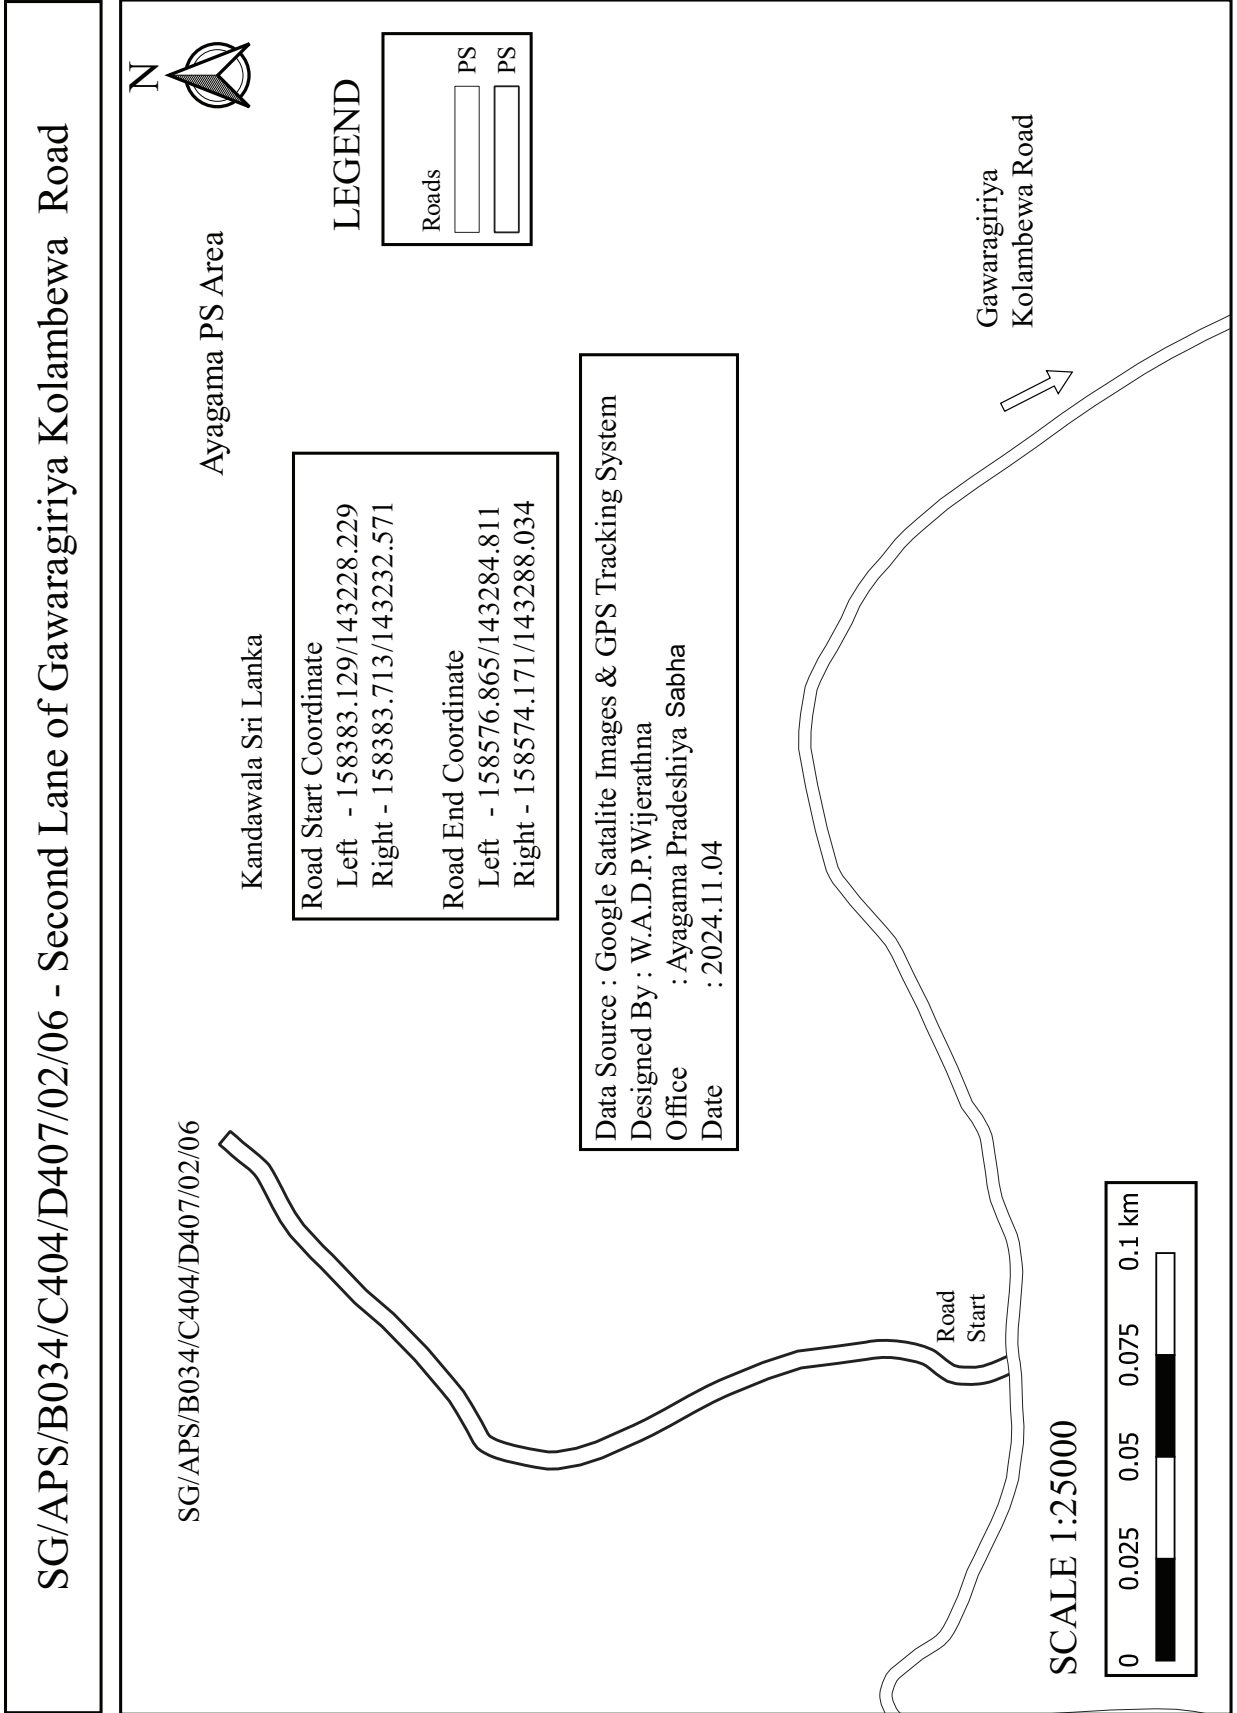


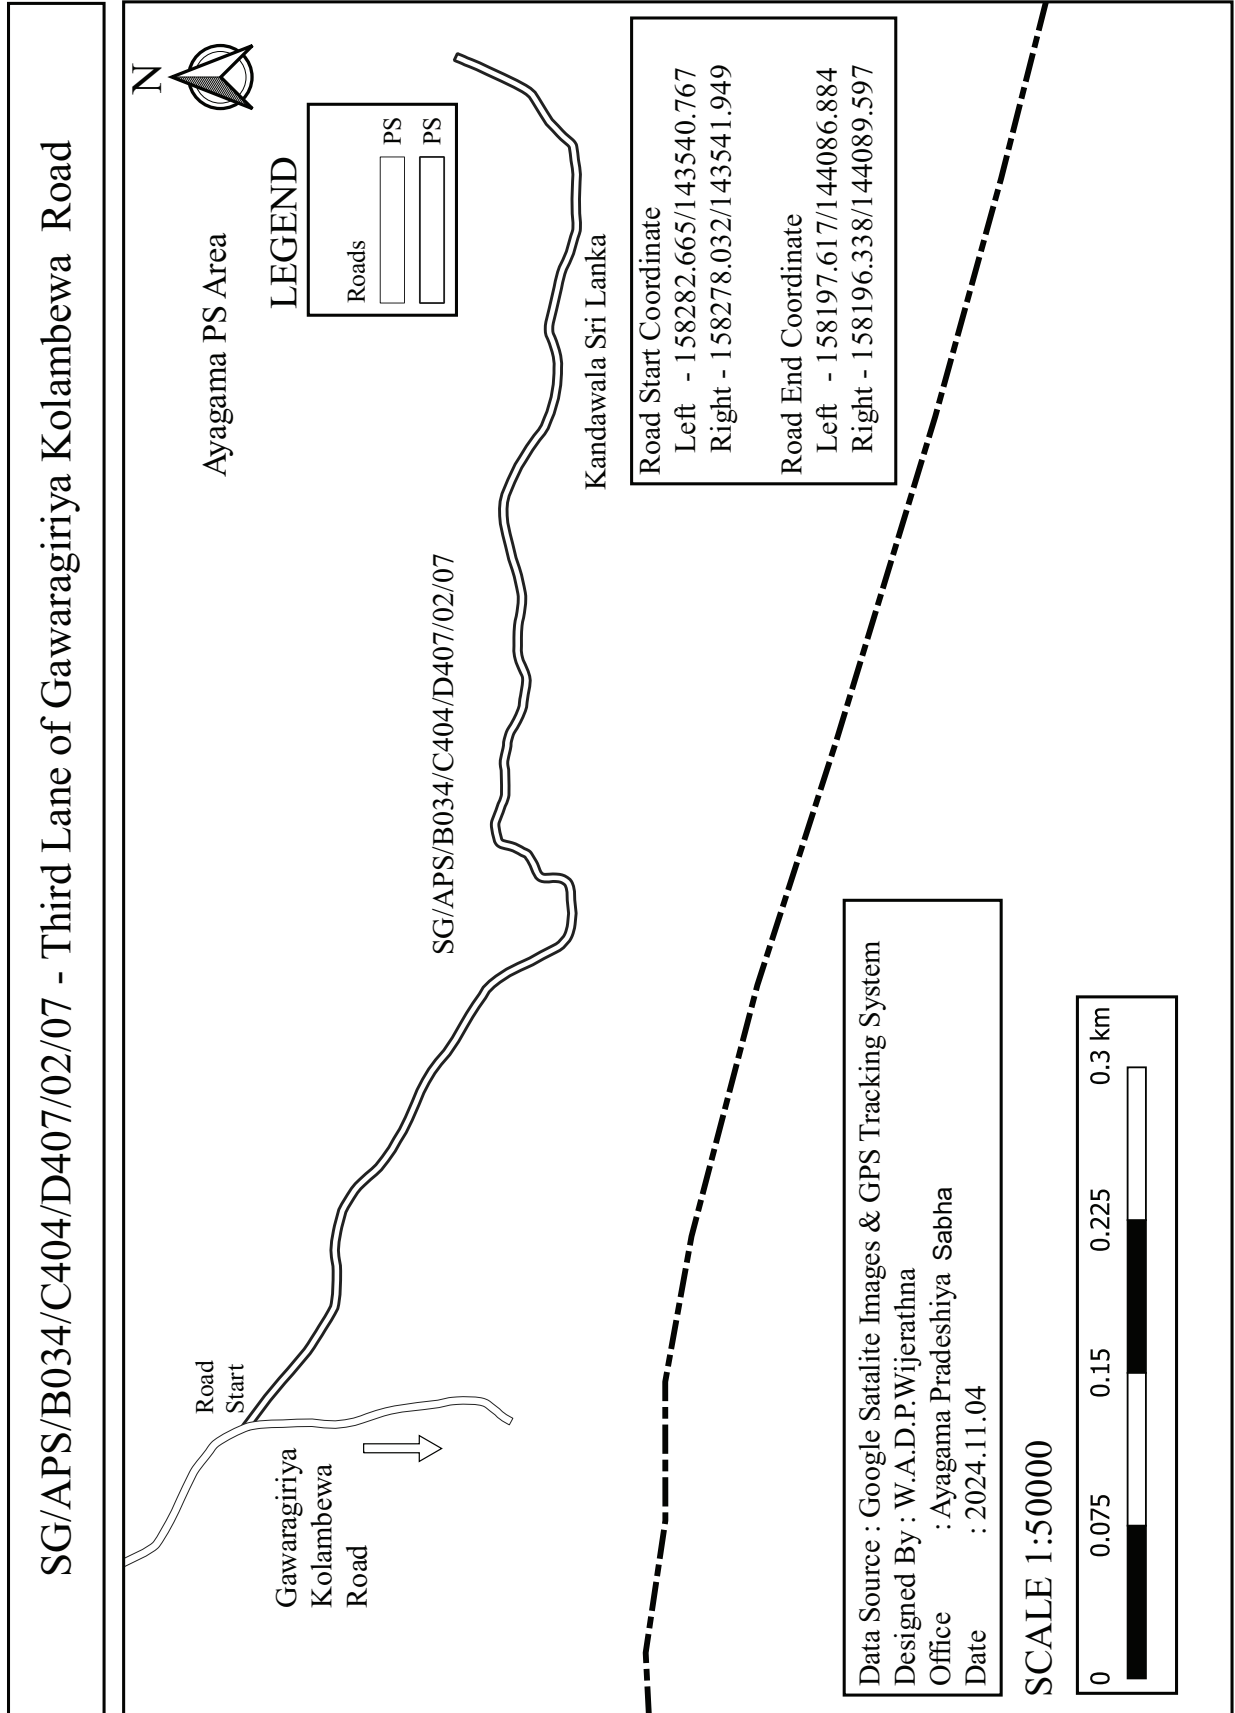


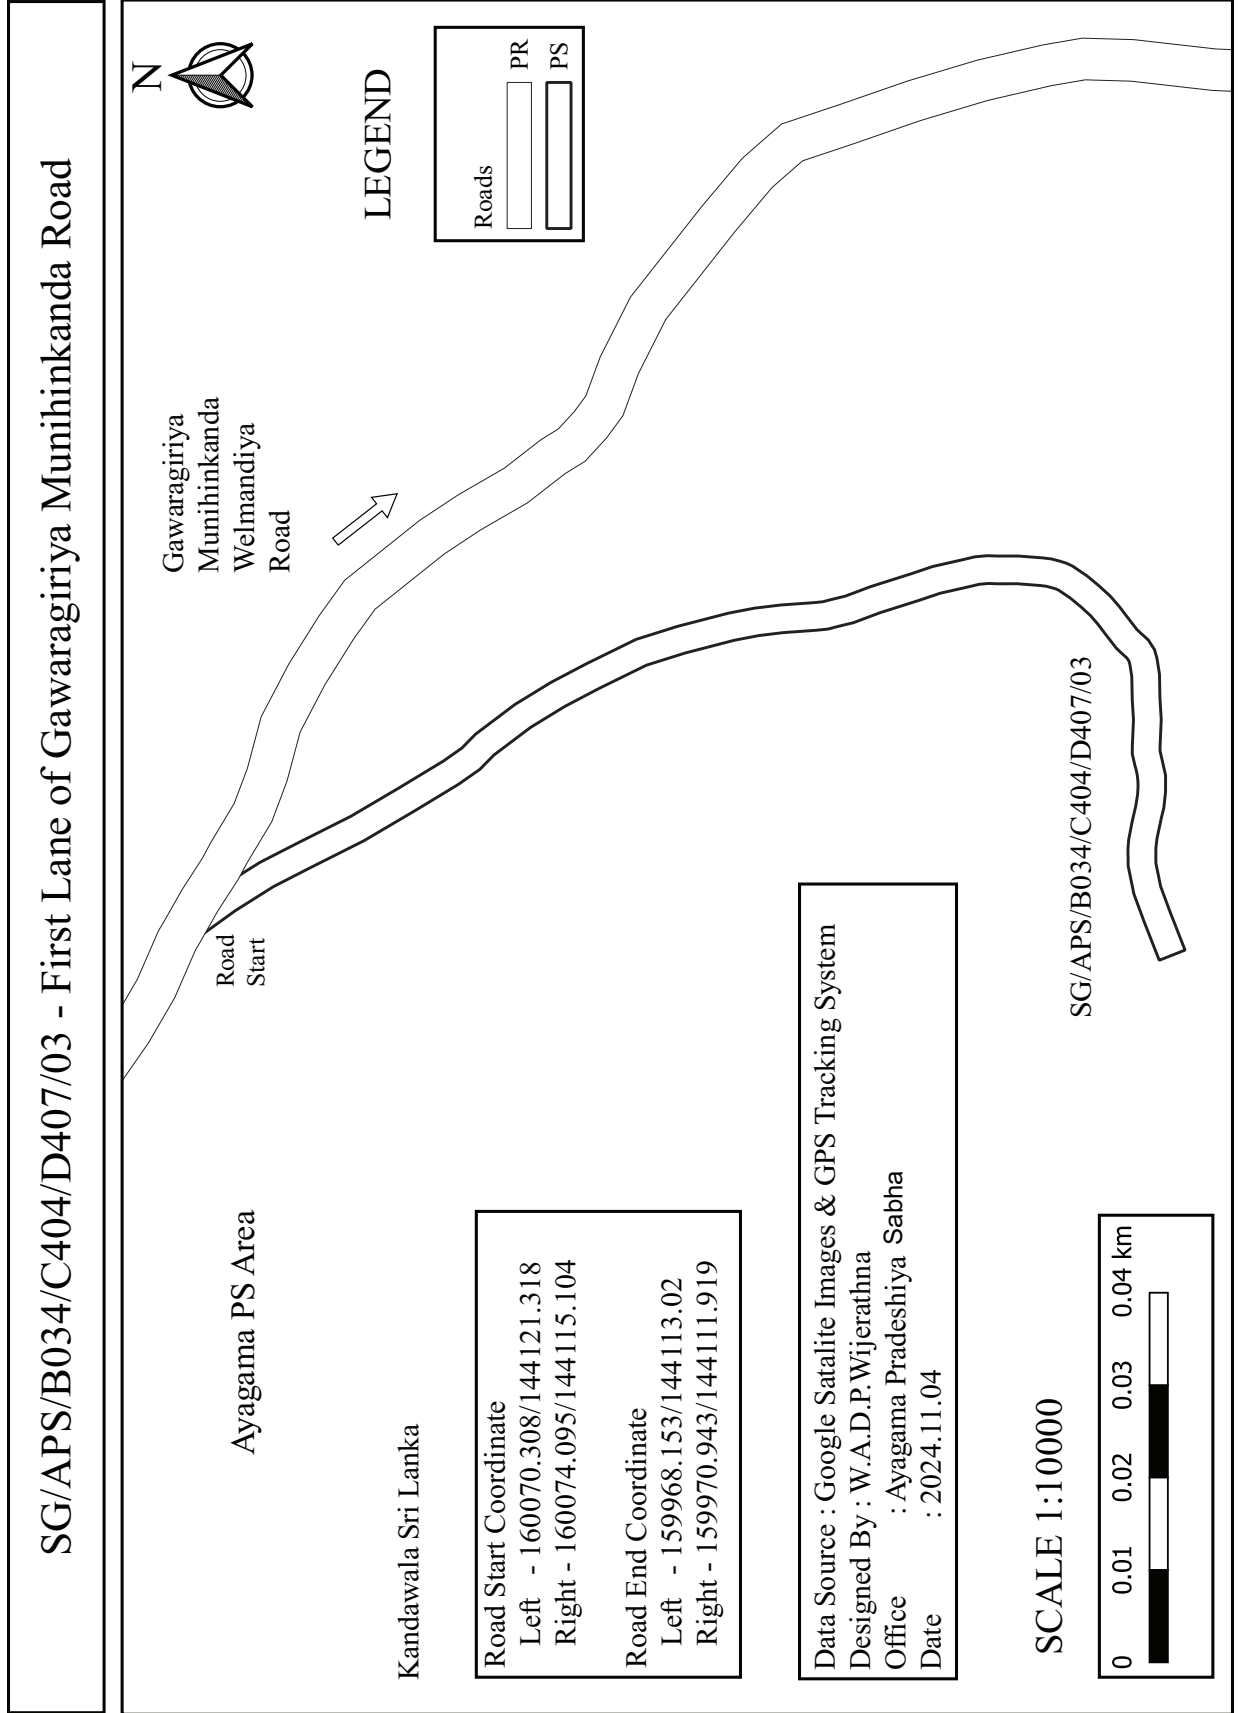


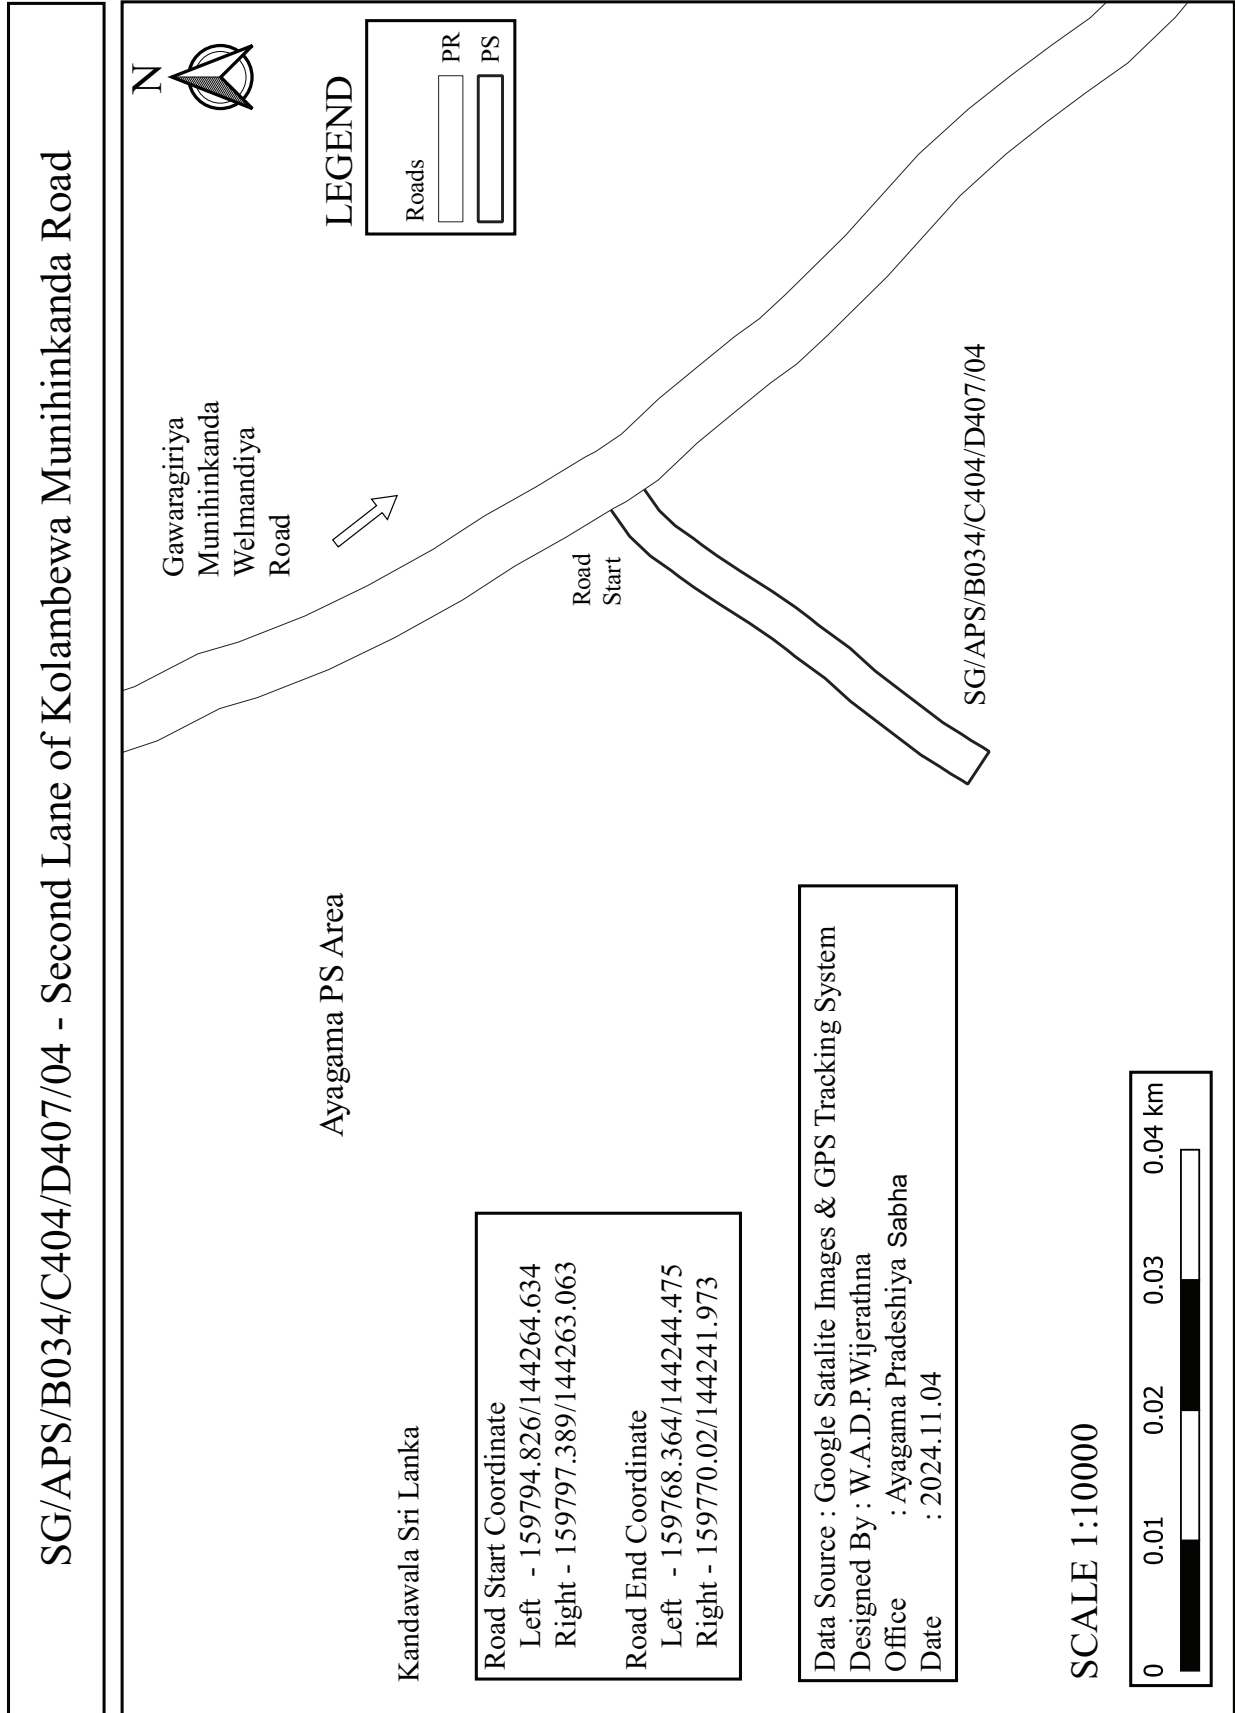


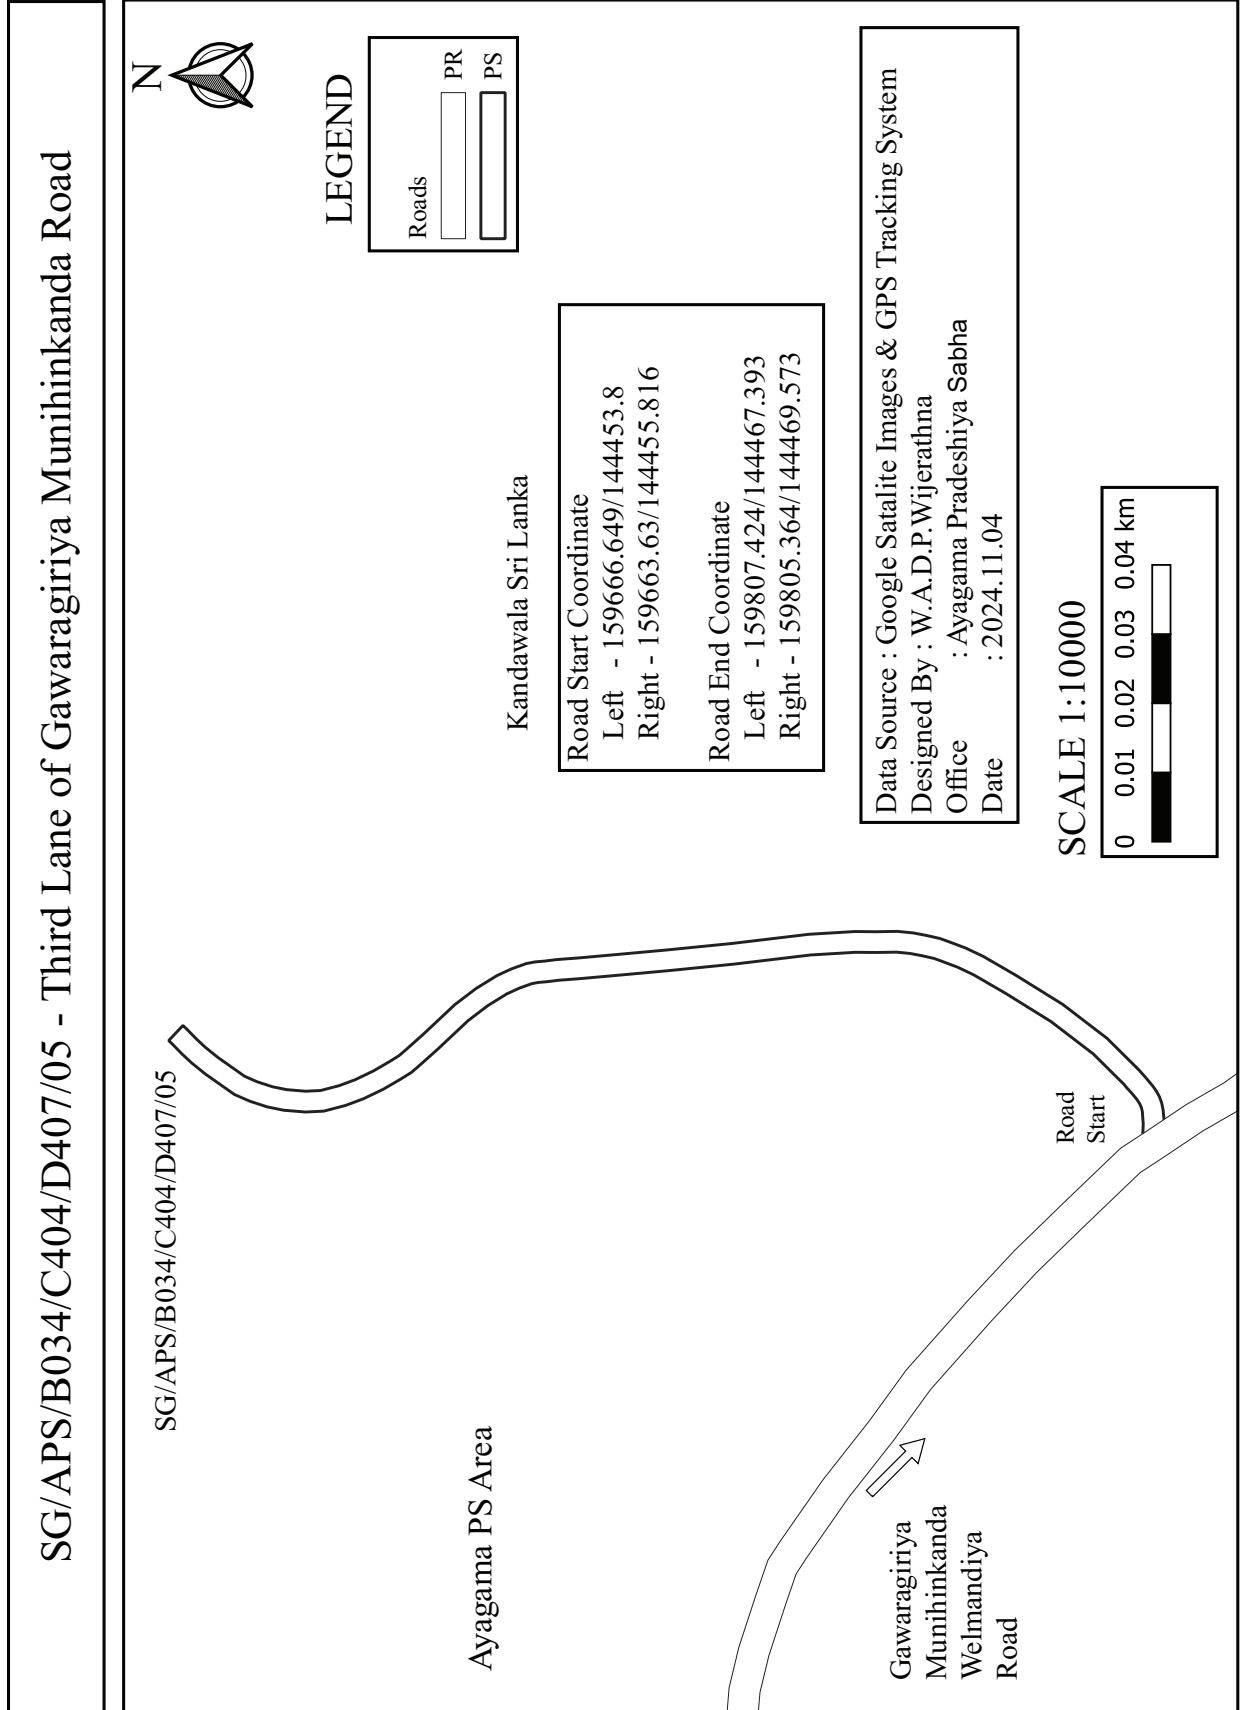


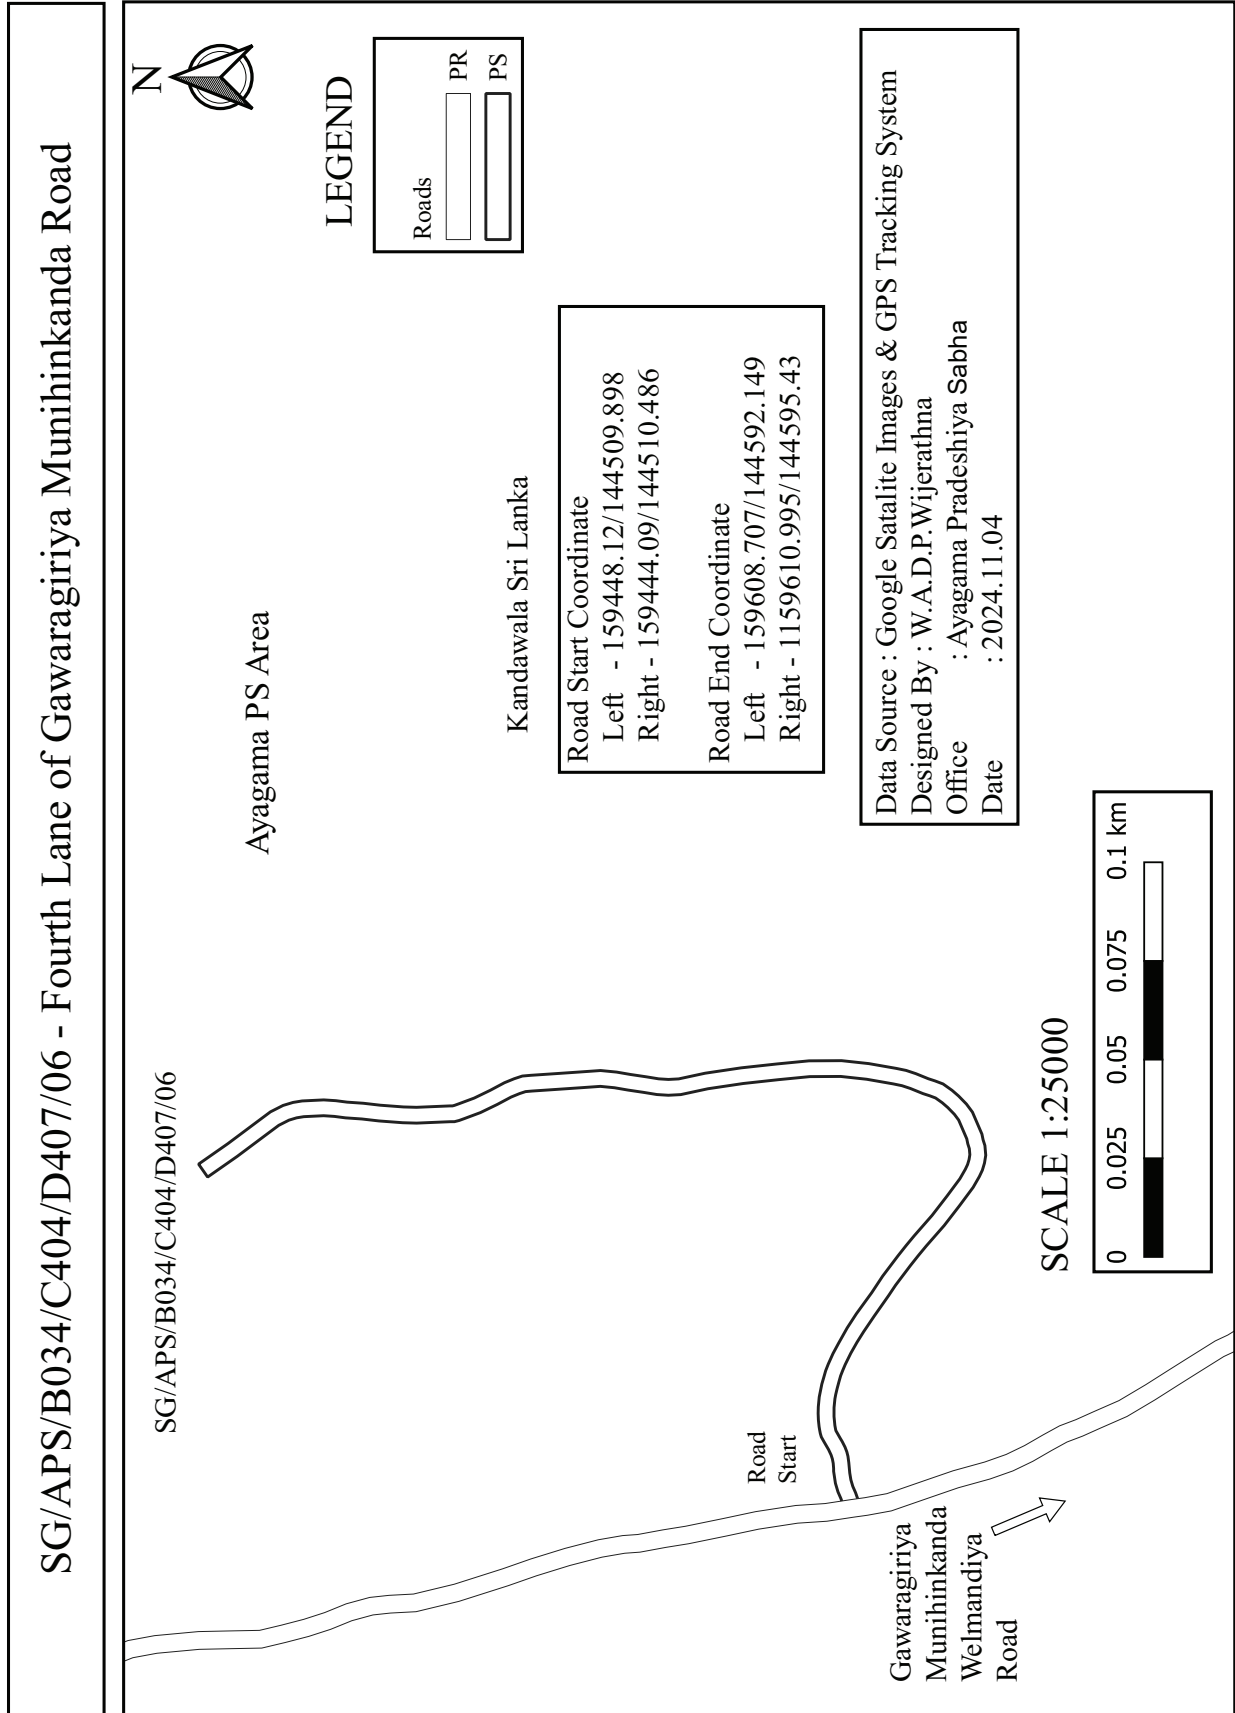


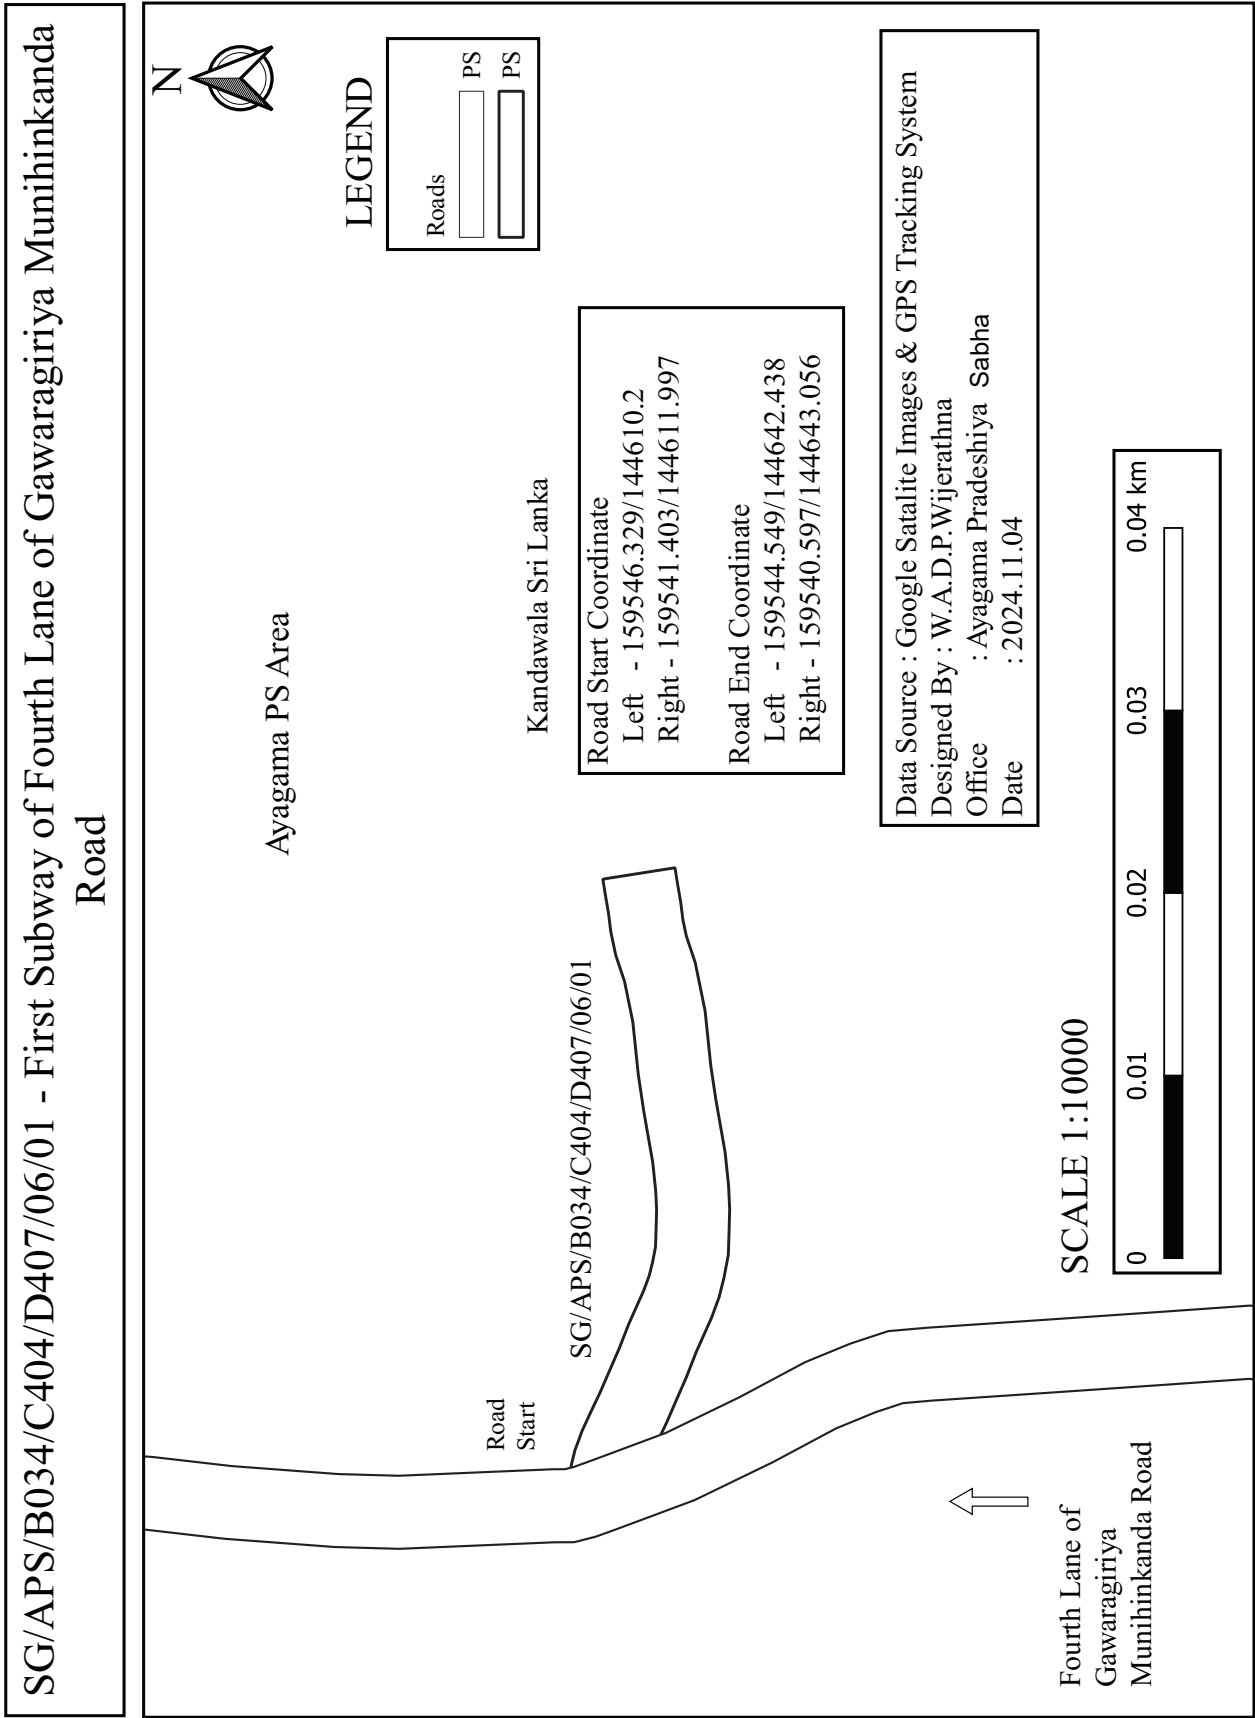


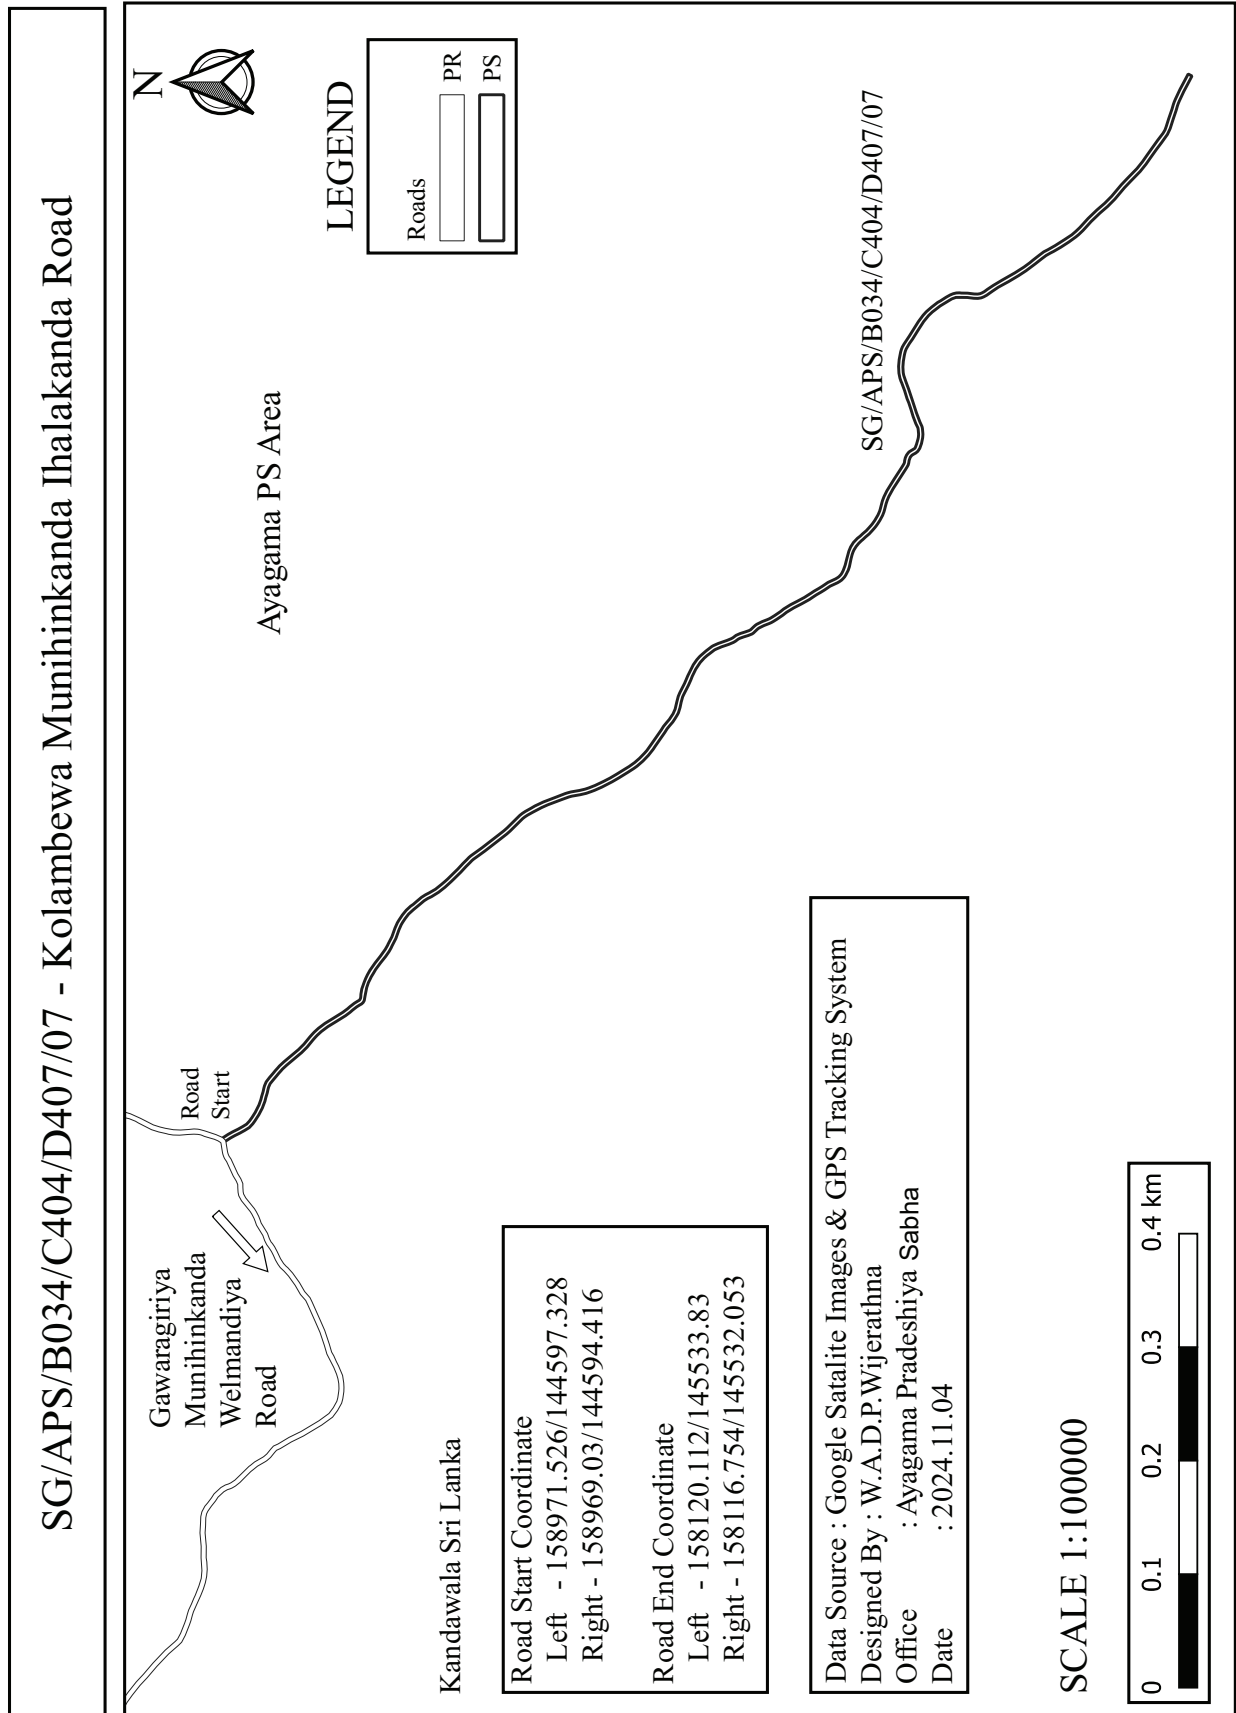


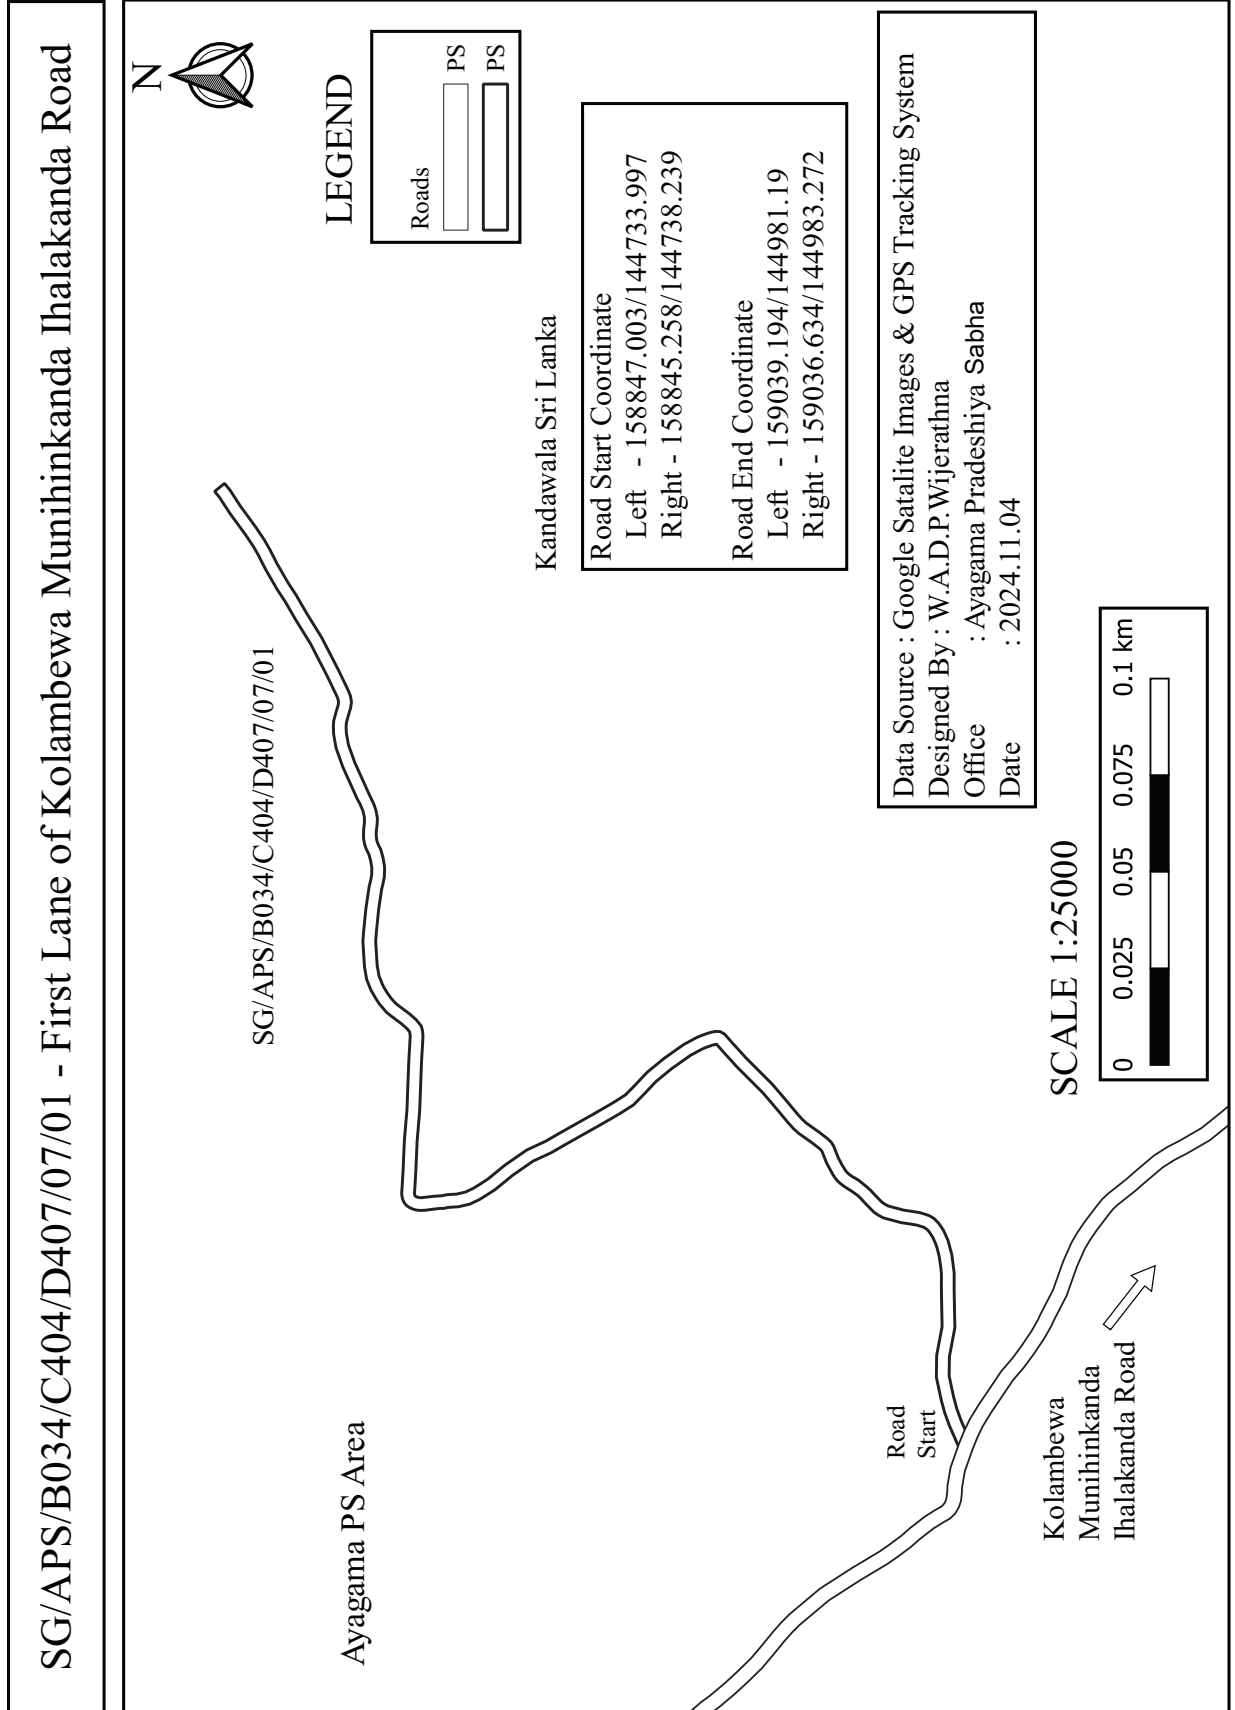


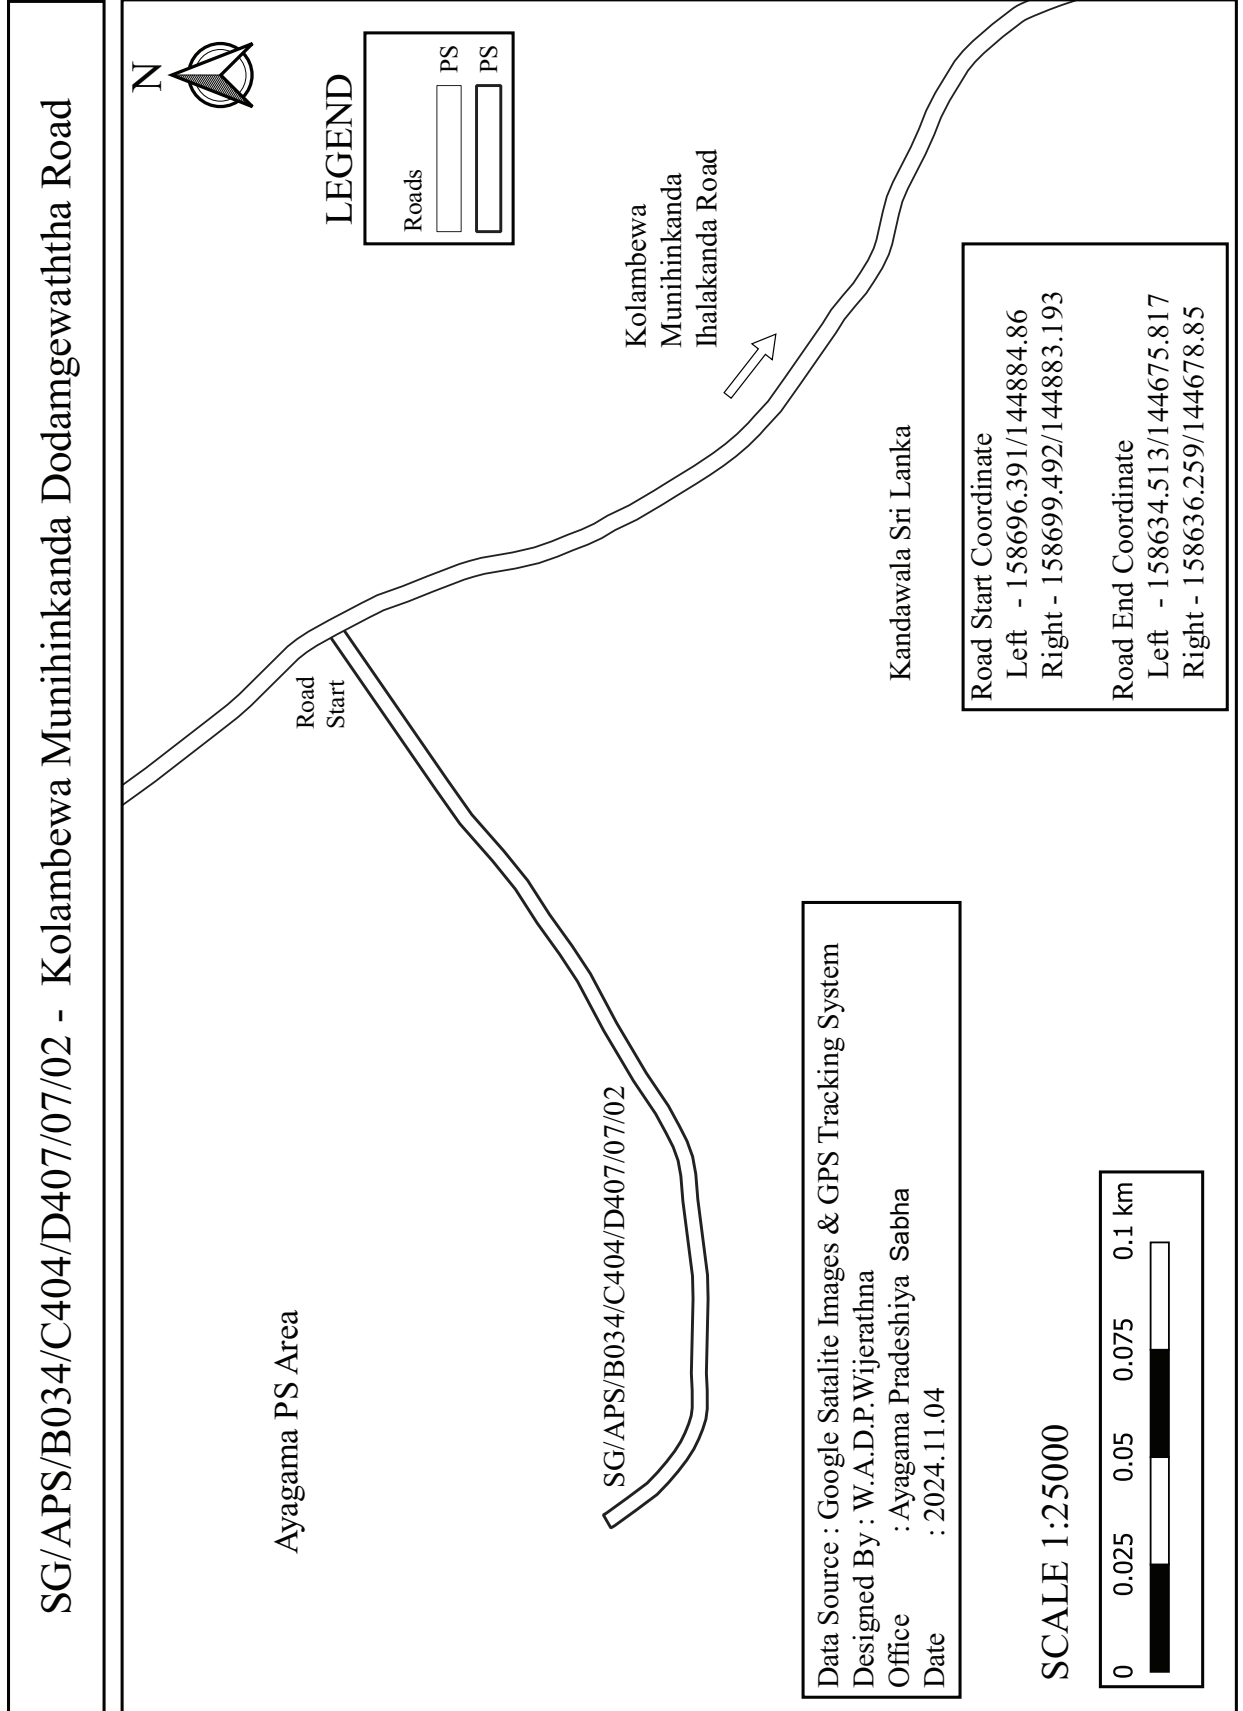


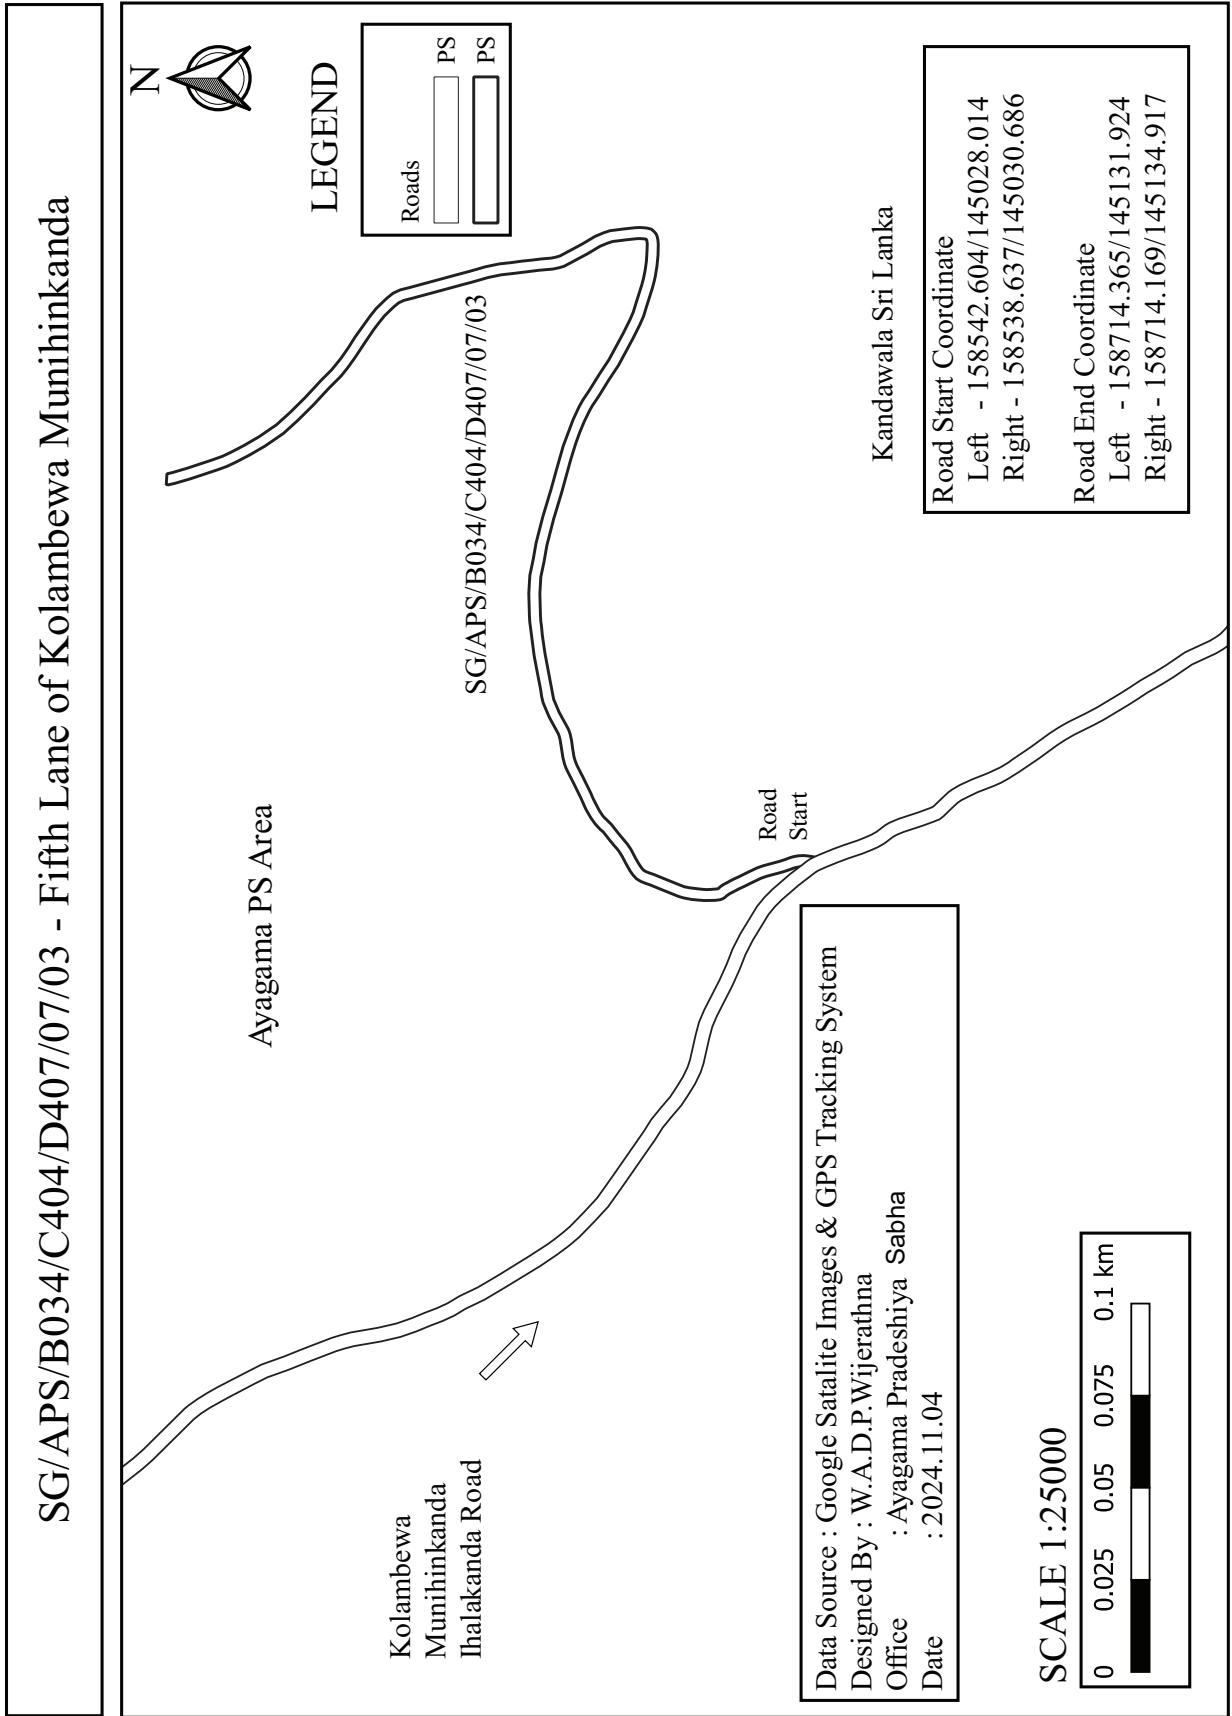


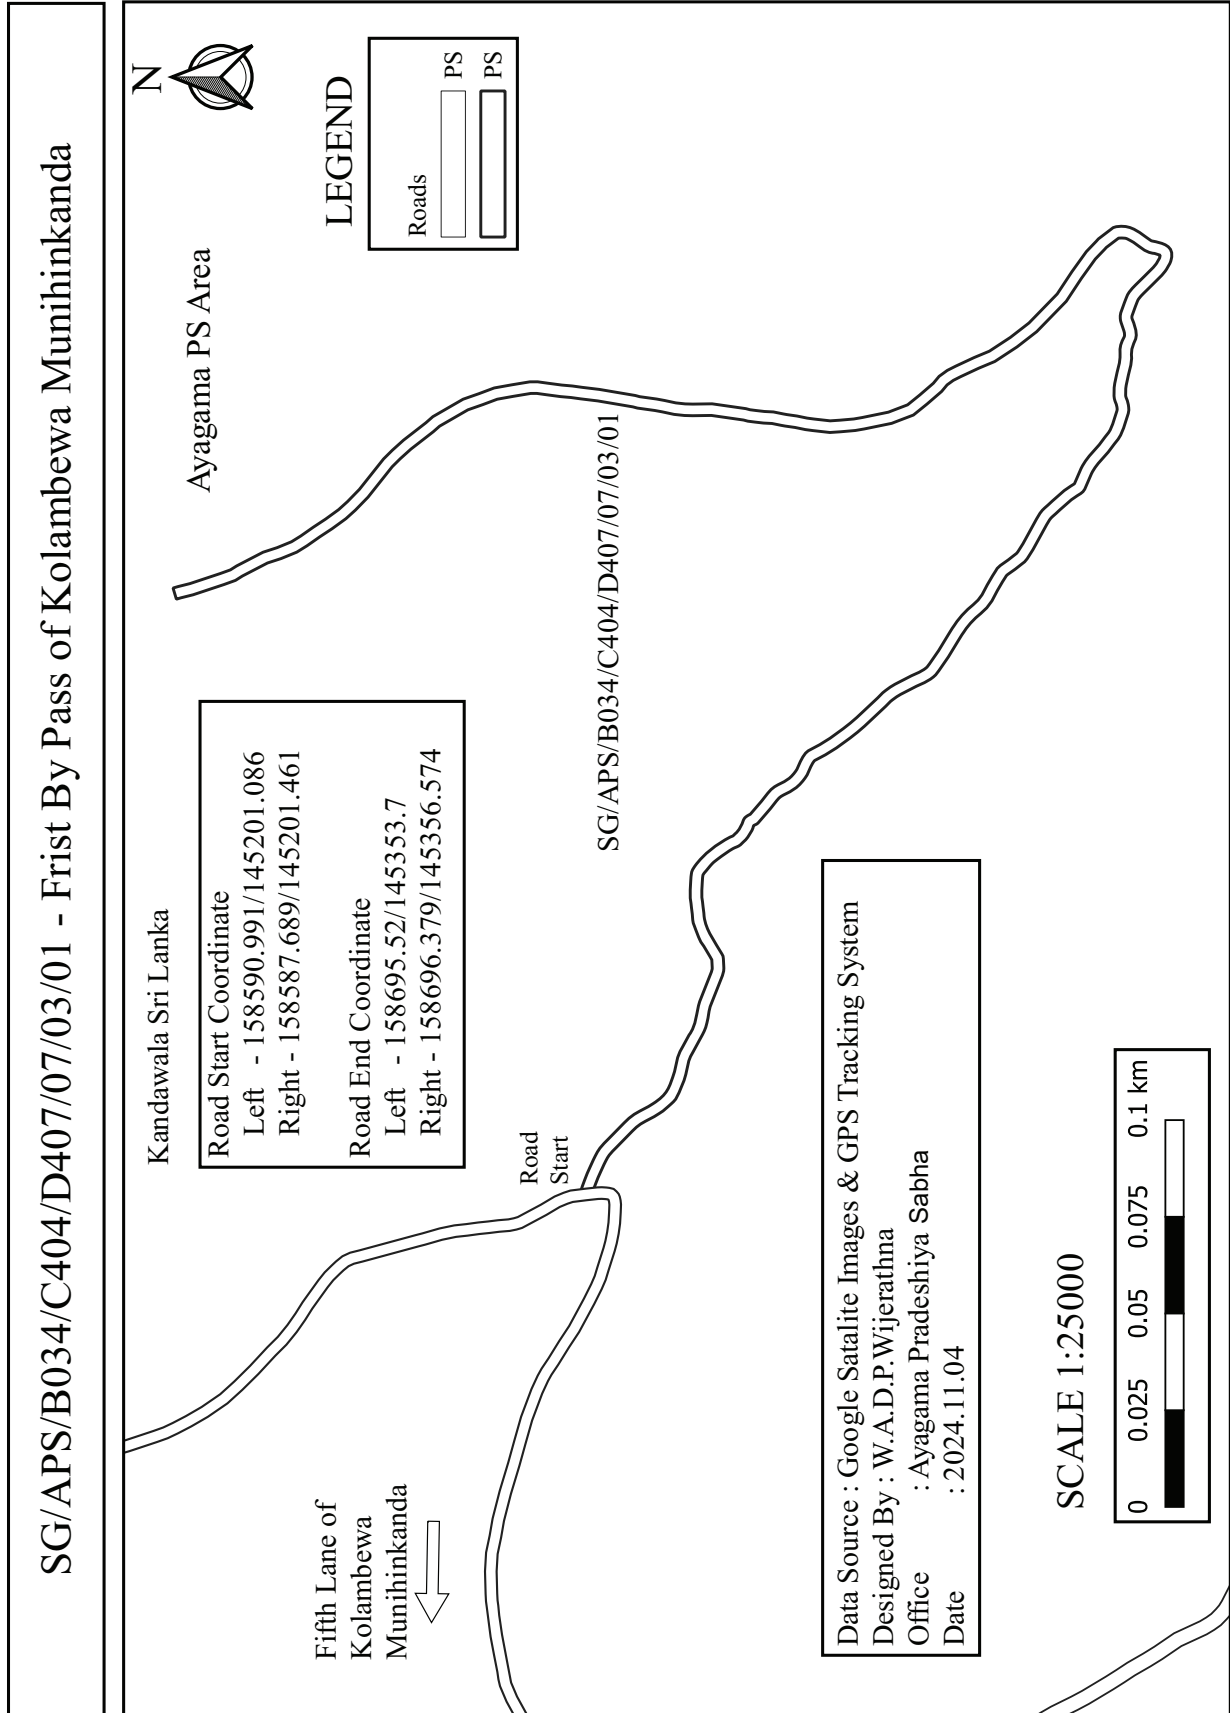


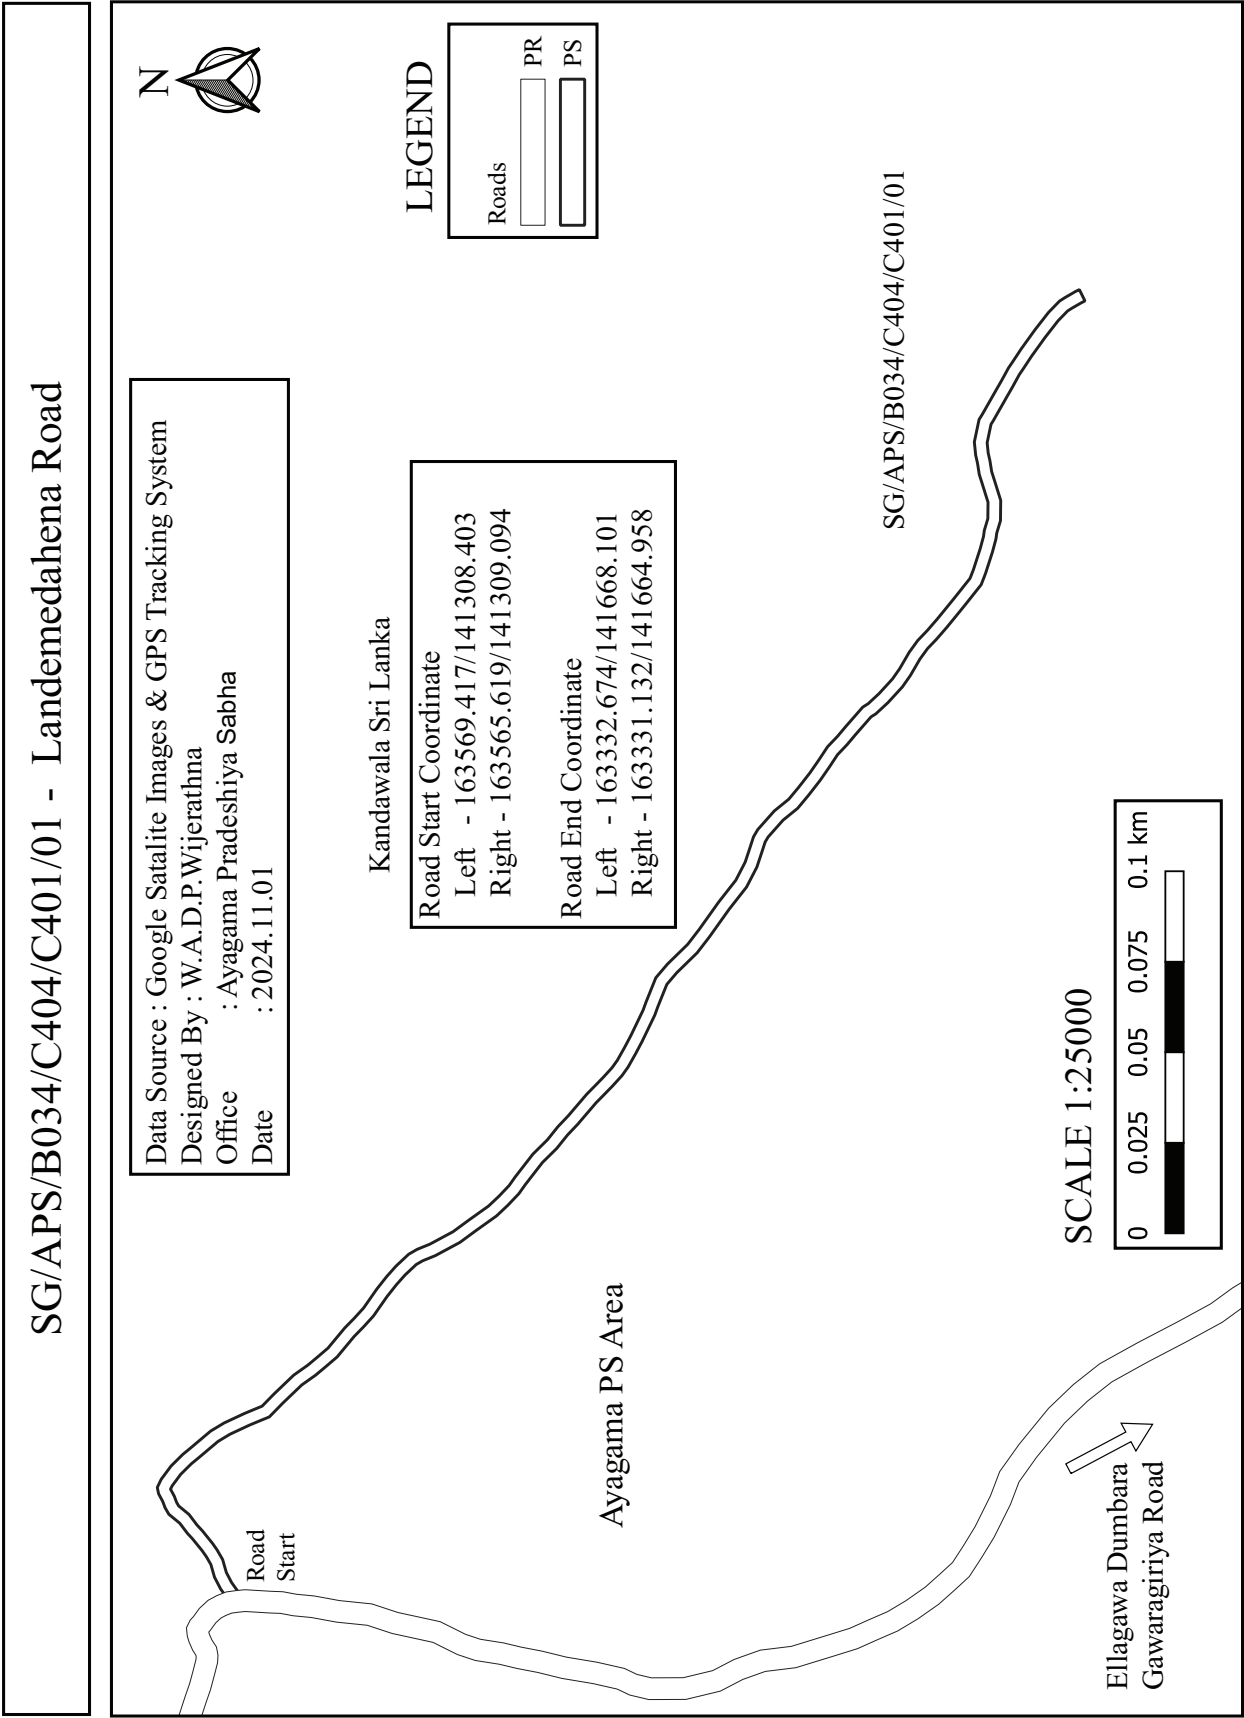

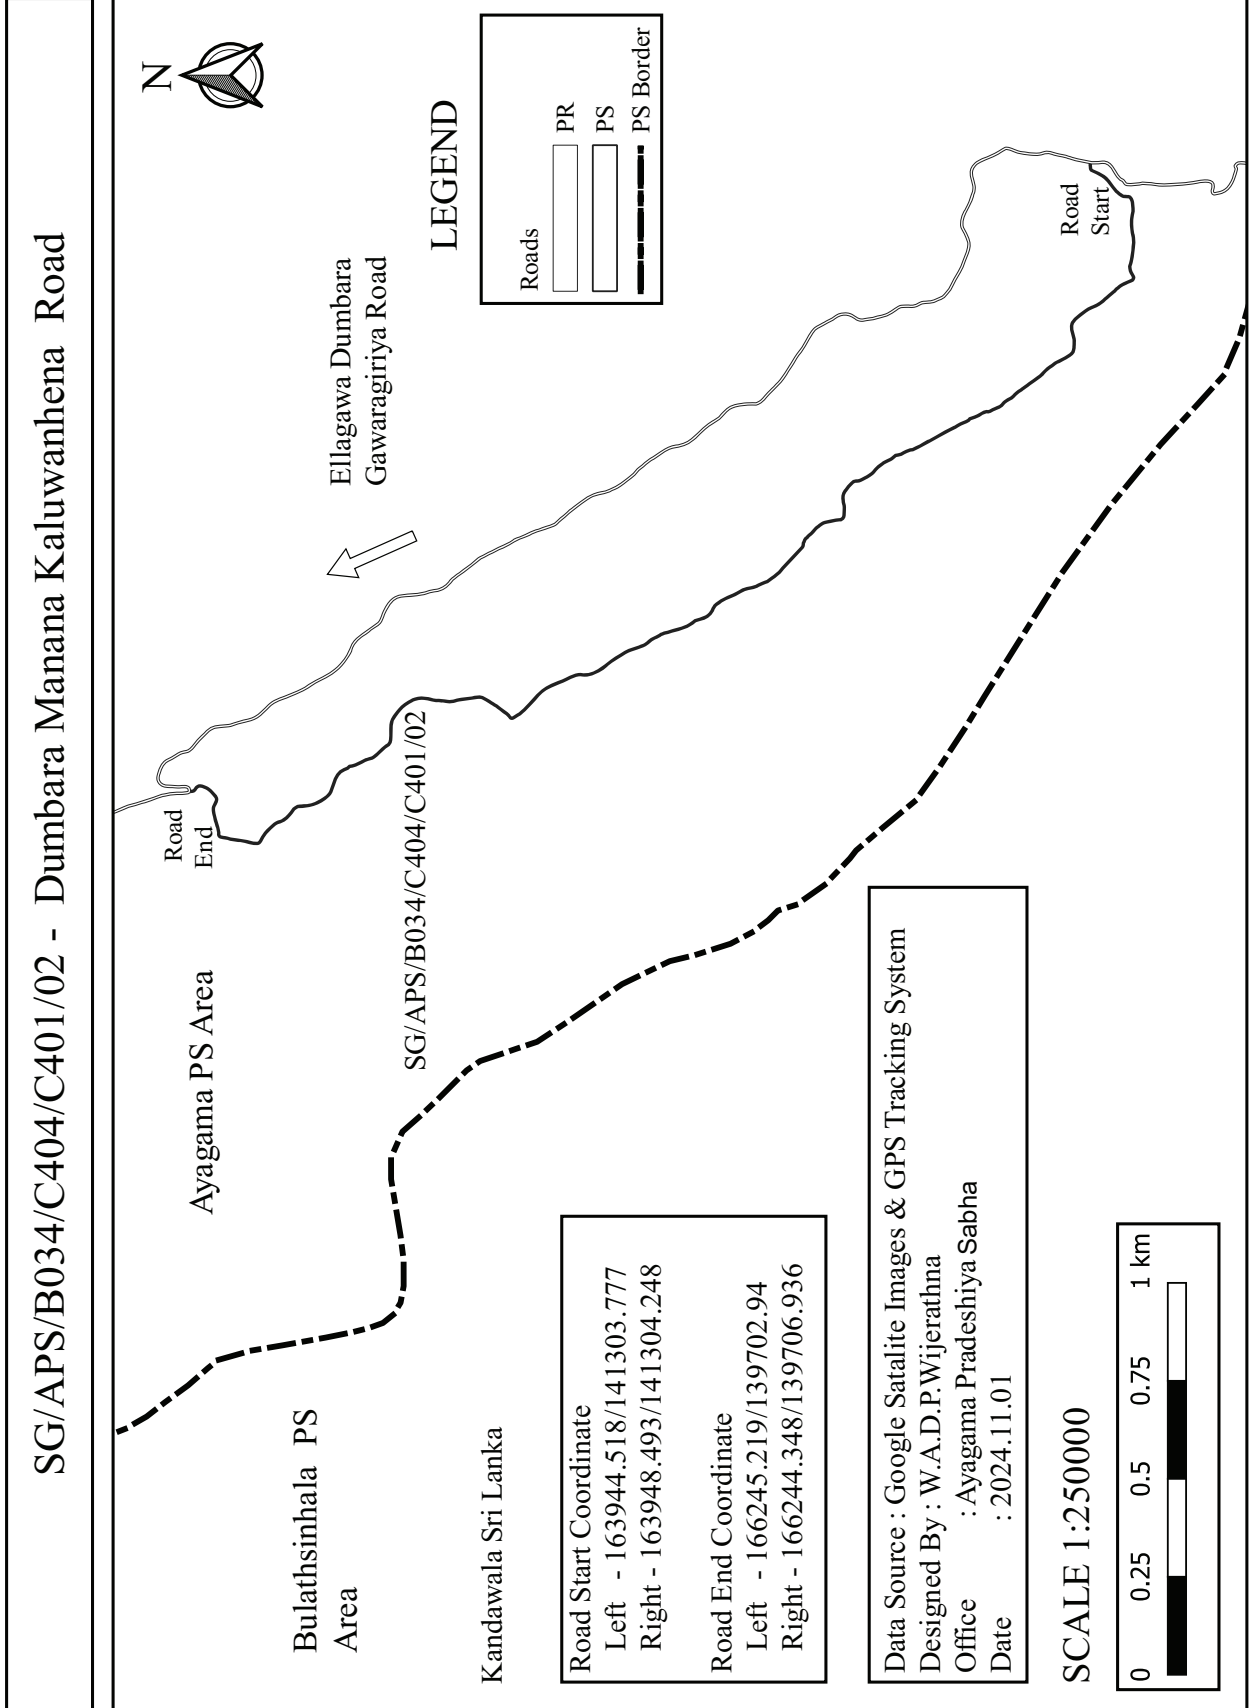


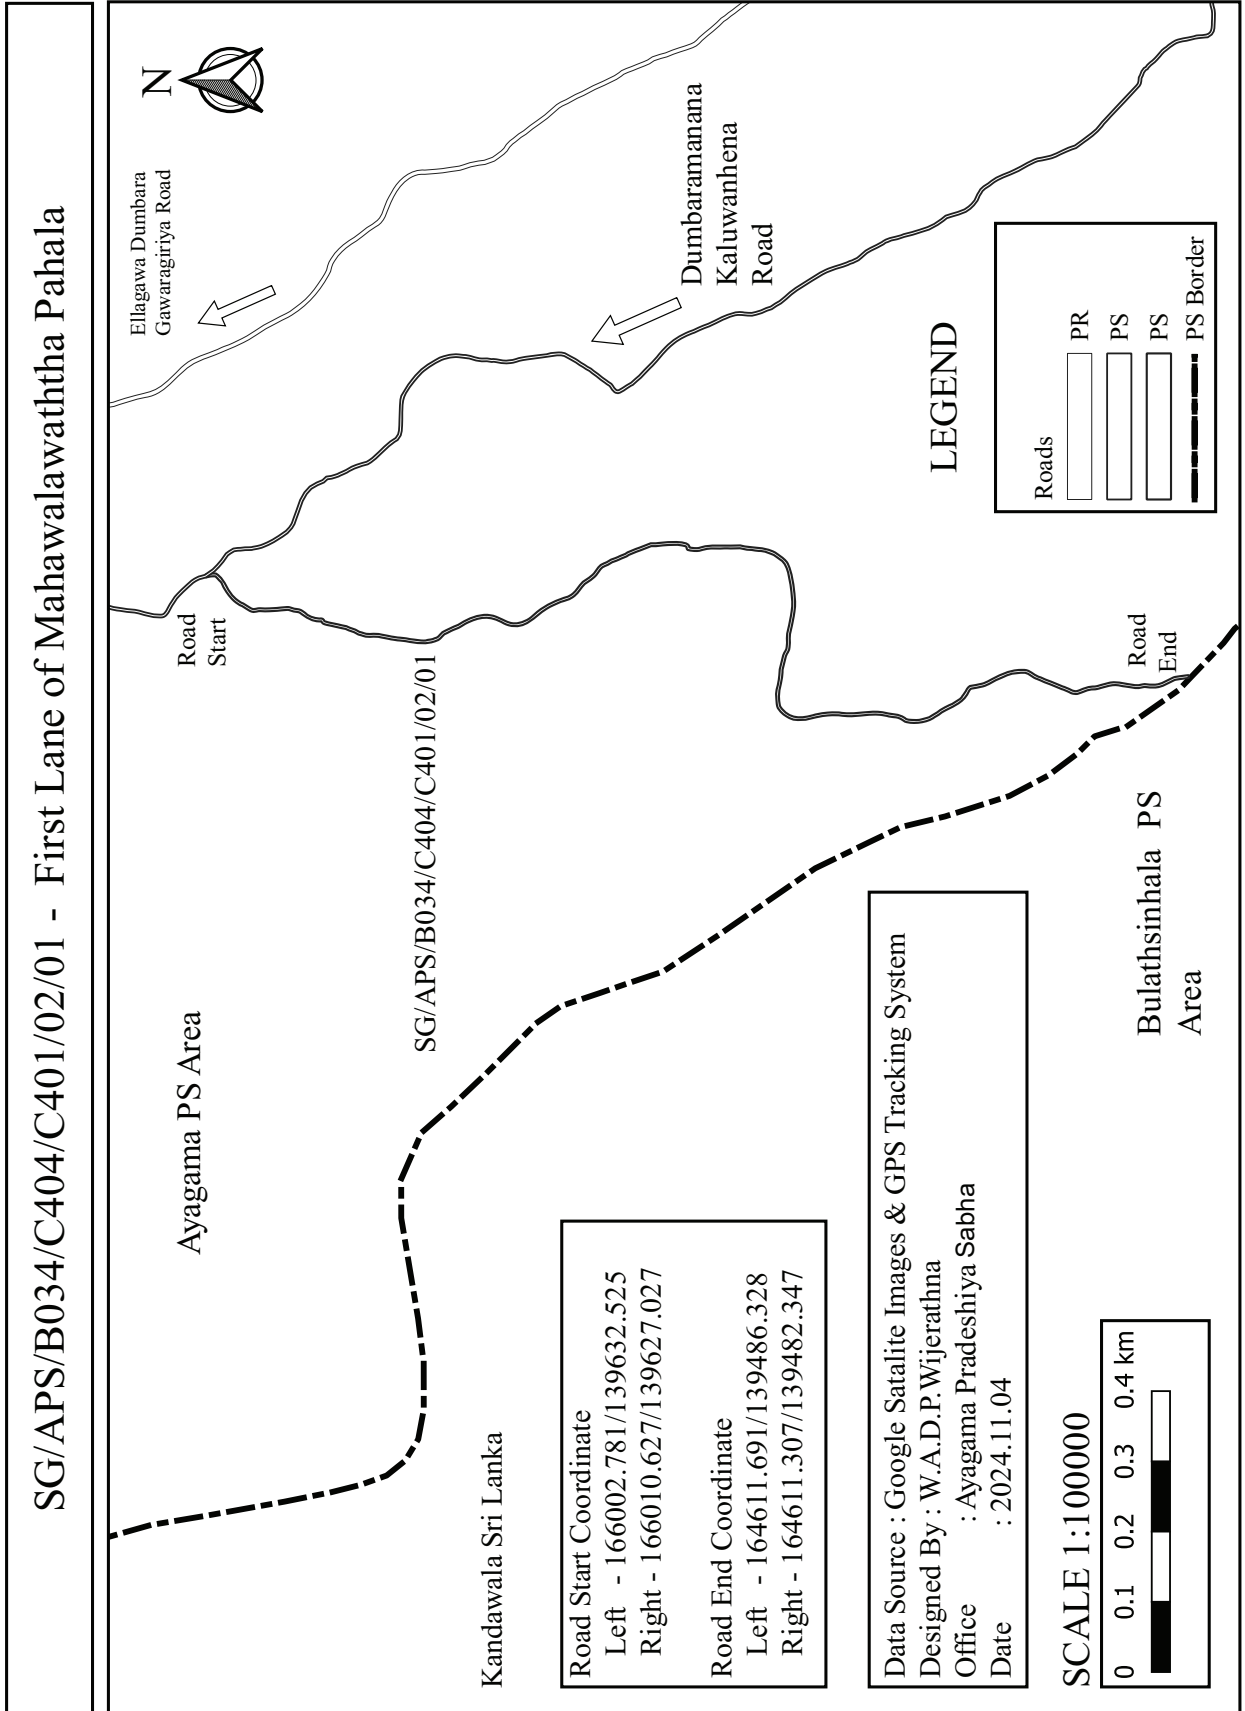


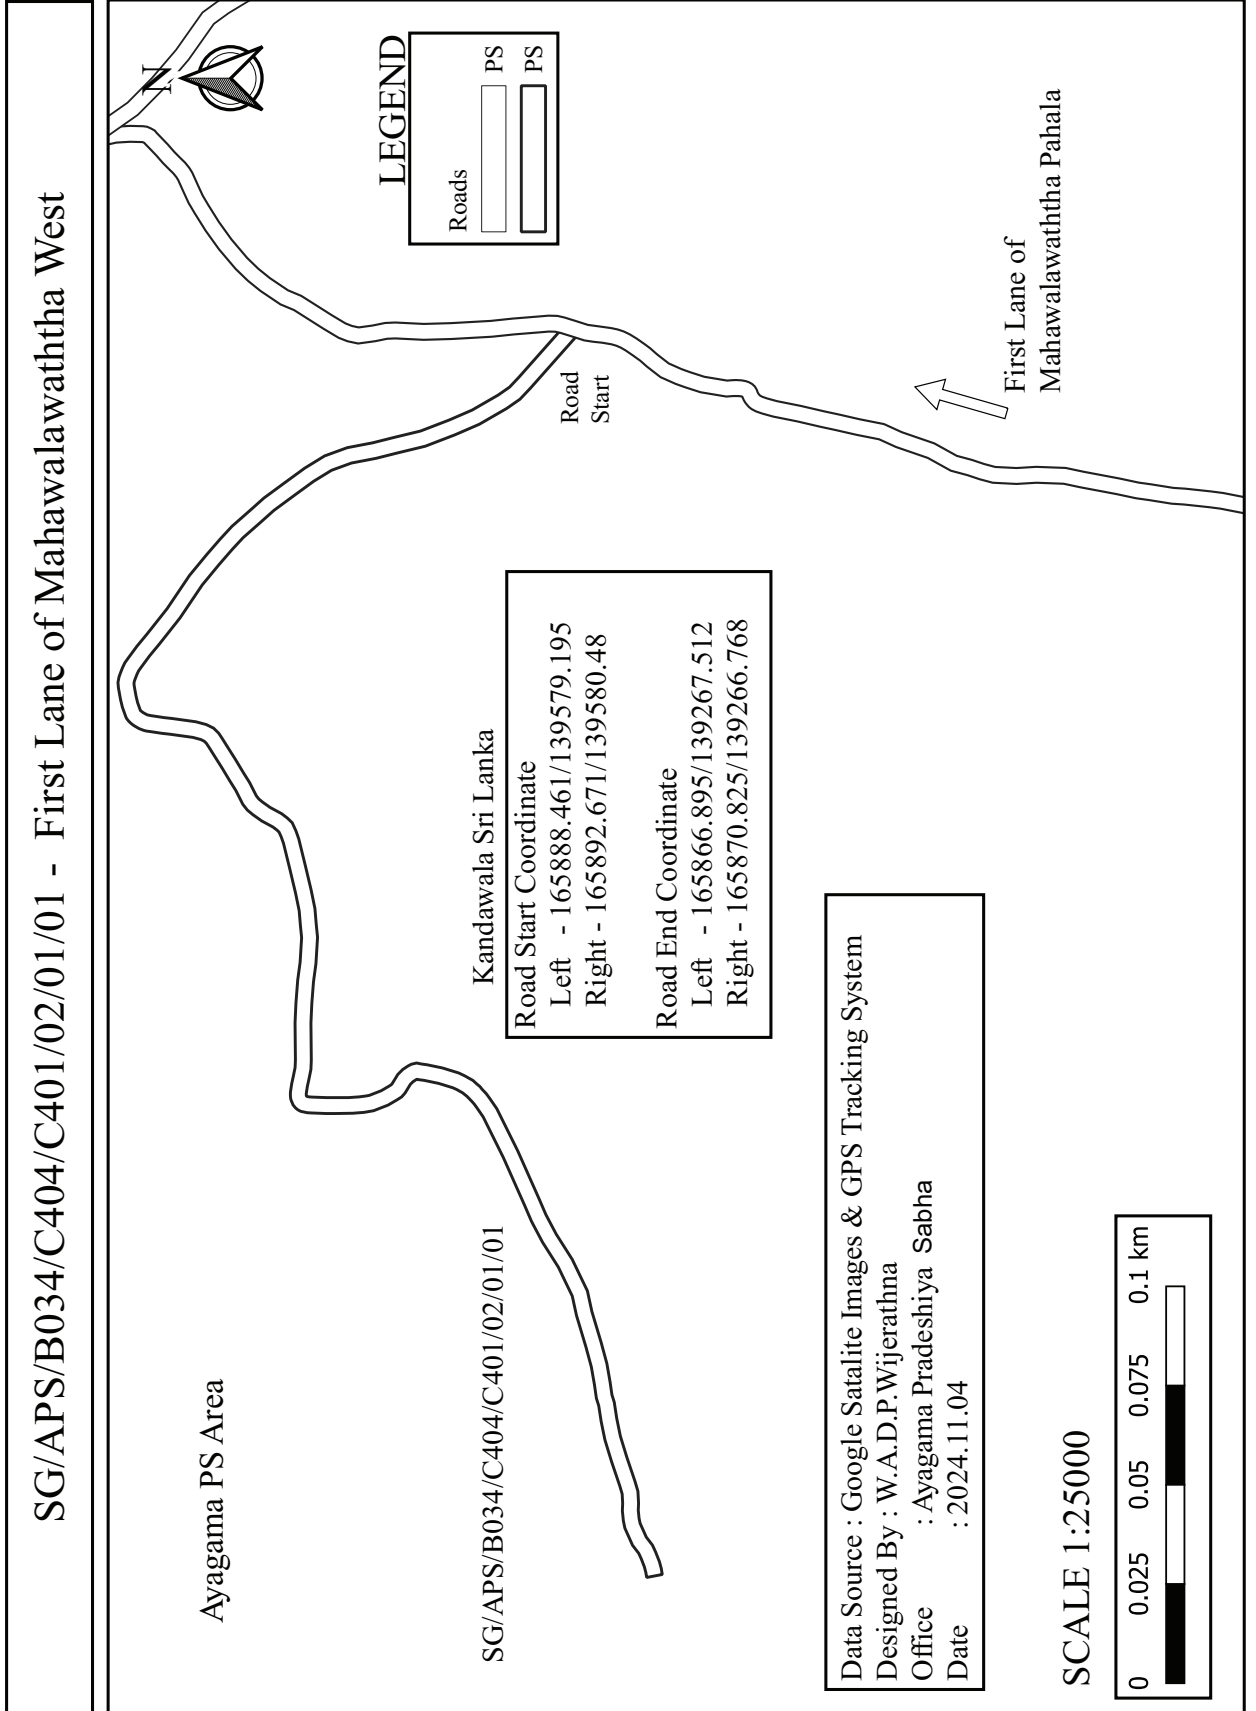

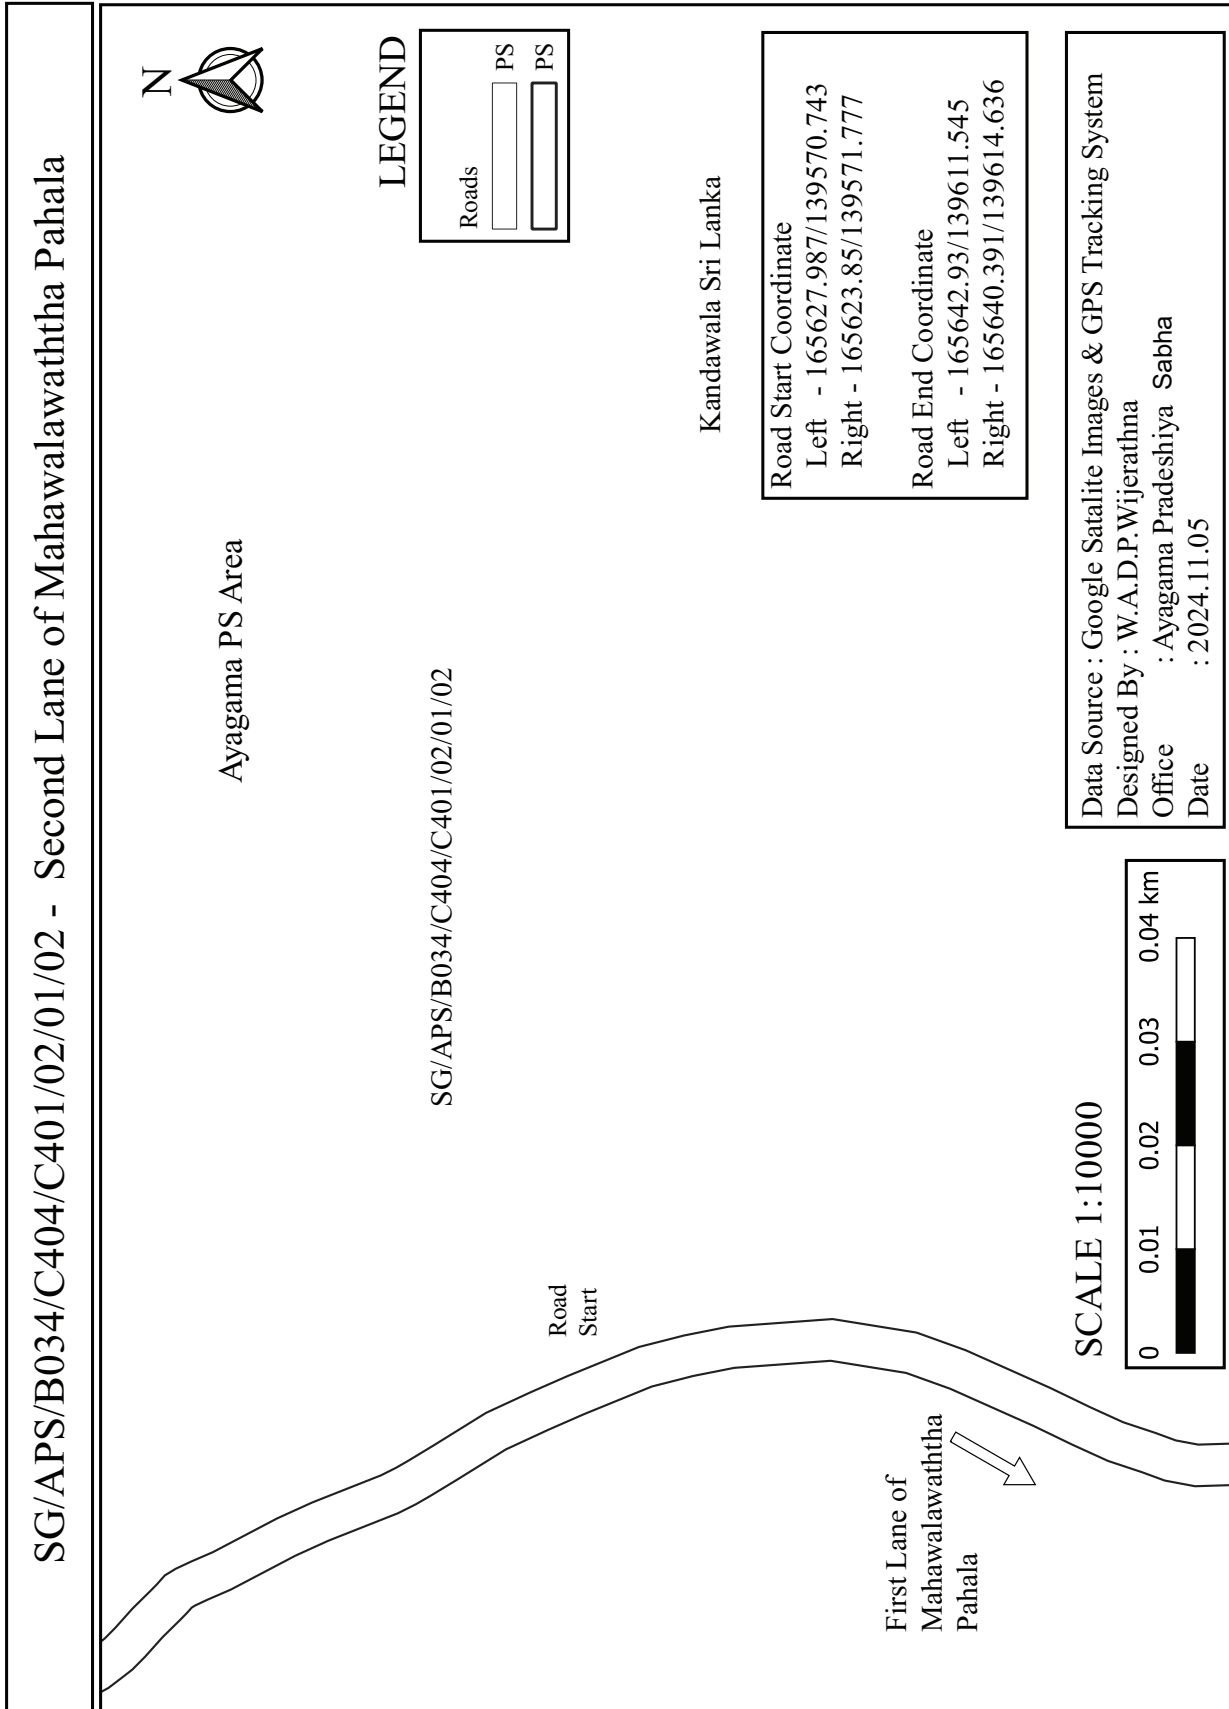



SG/APS/B034/C404/C401/02/01/03 - Second Lane of Mahawalawaththa West

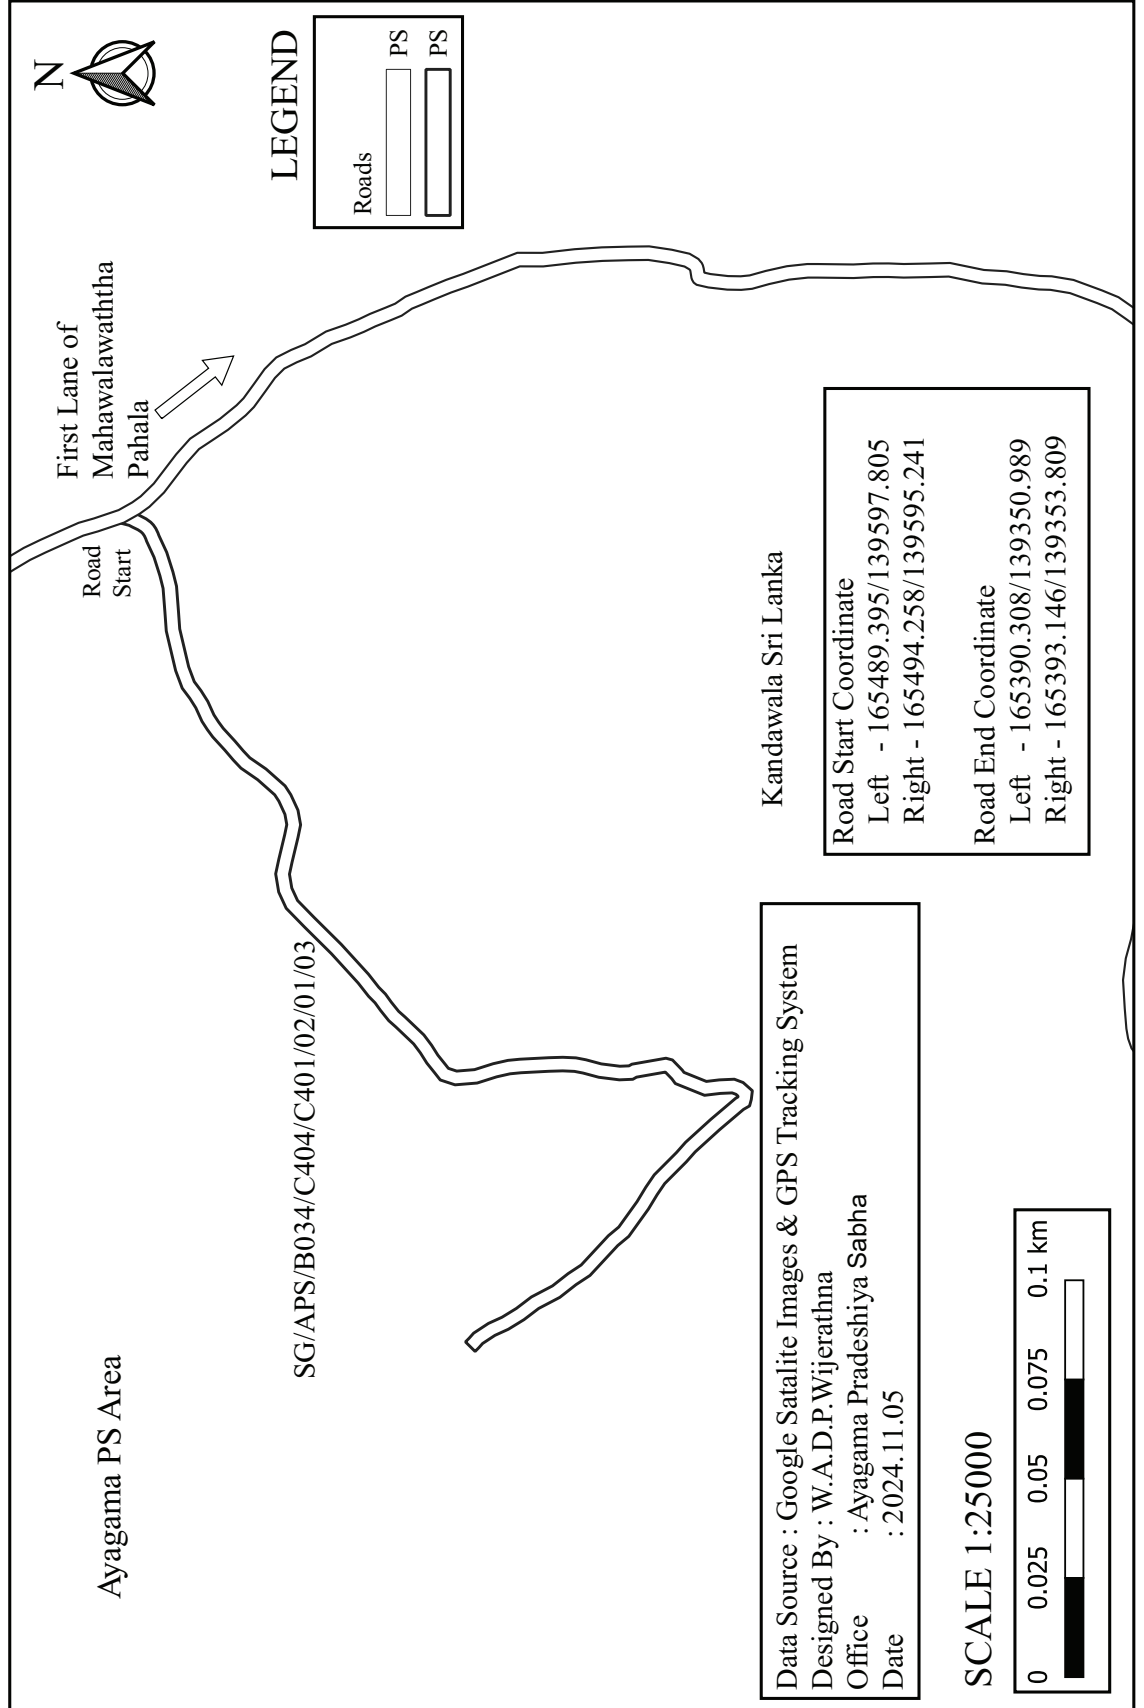


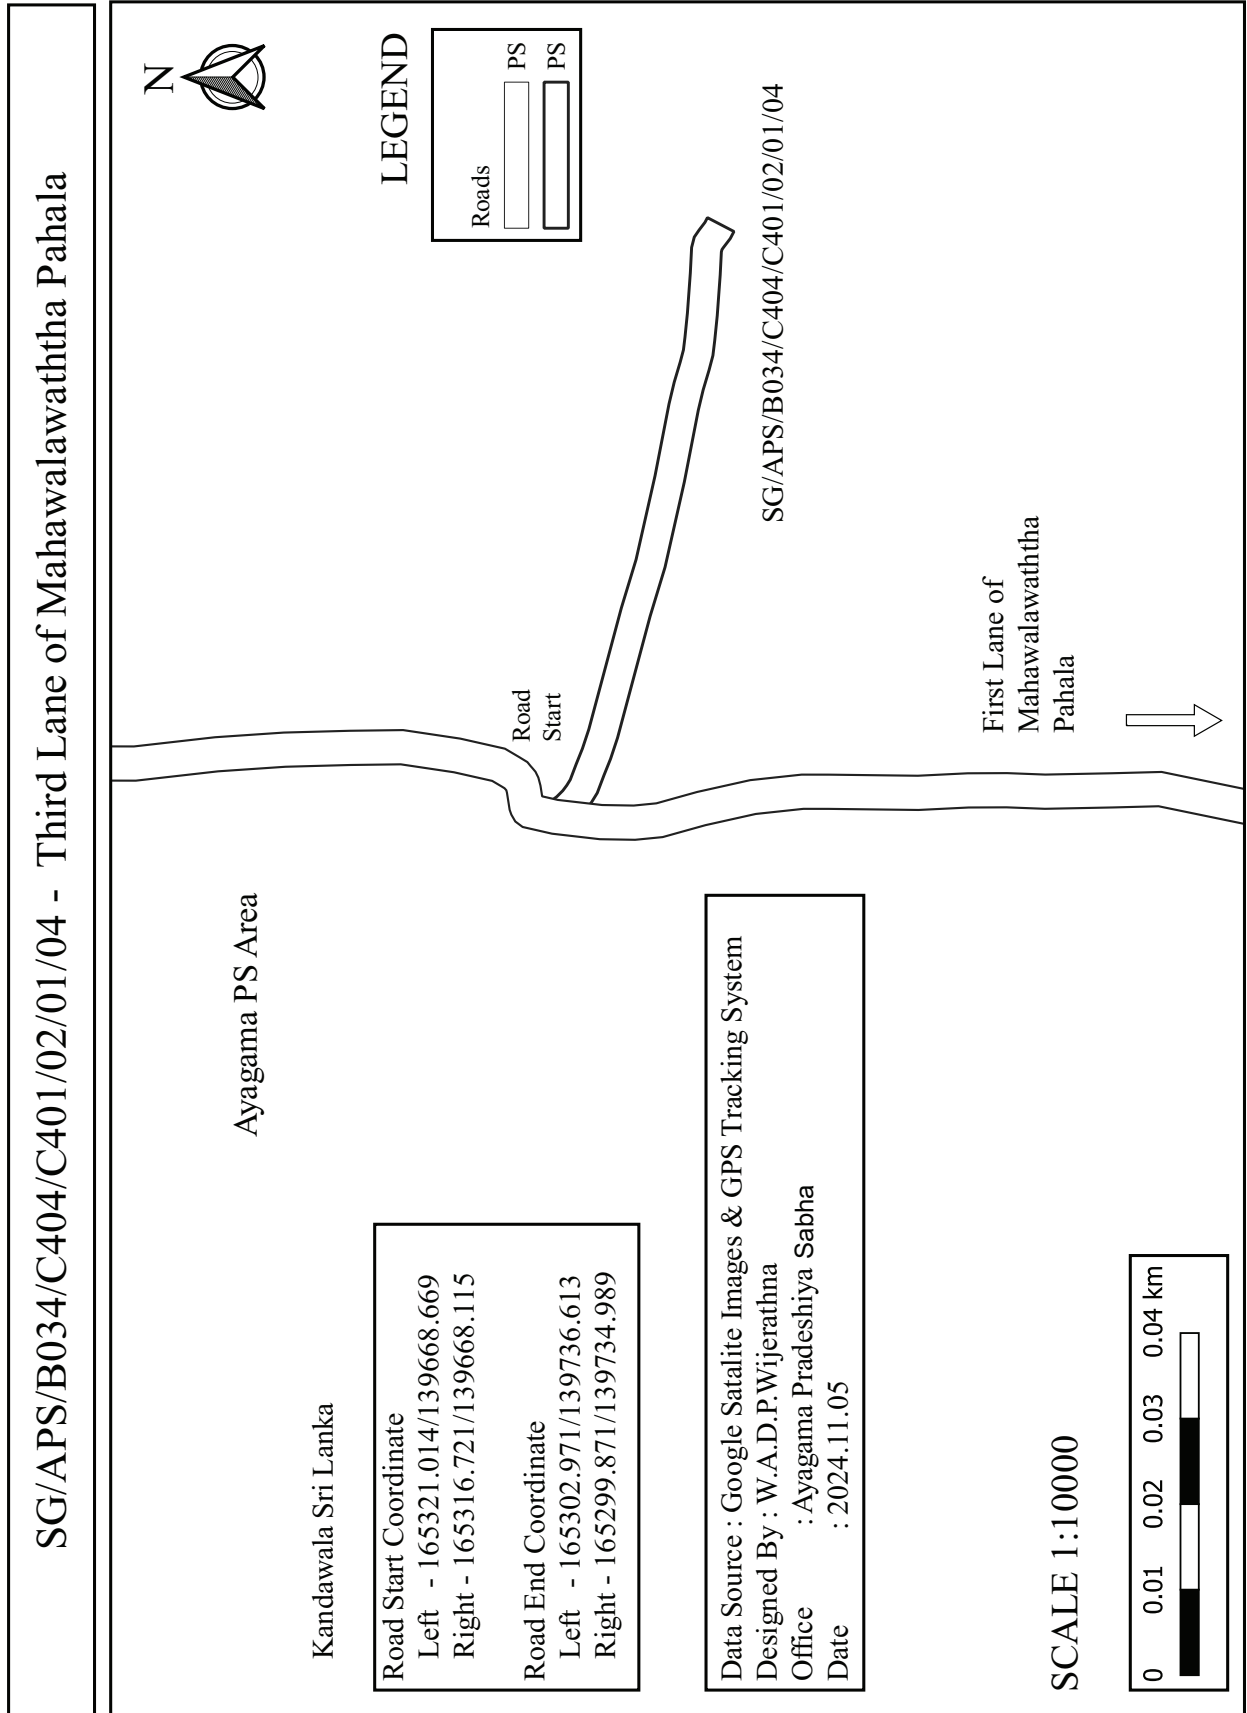


SG/APS/B034/C404/C401/02/01/05 - Sodurukanda Road

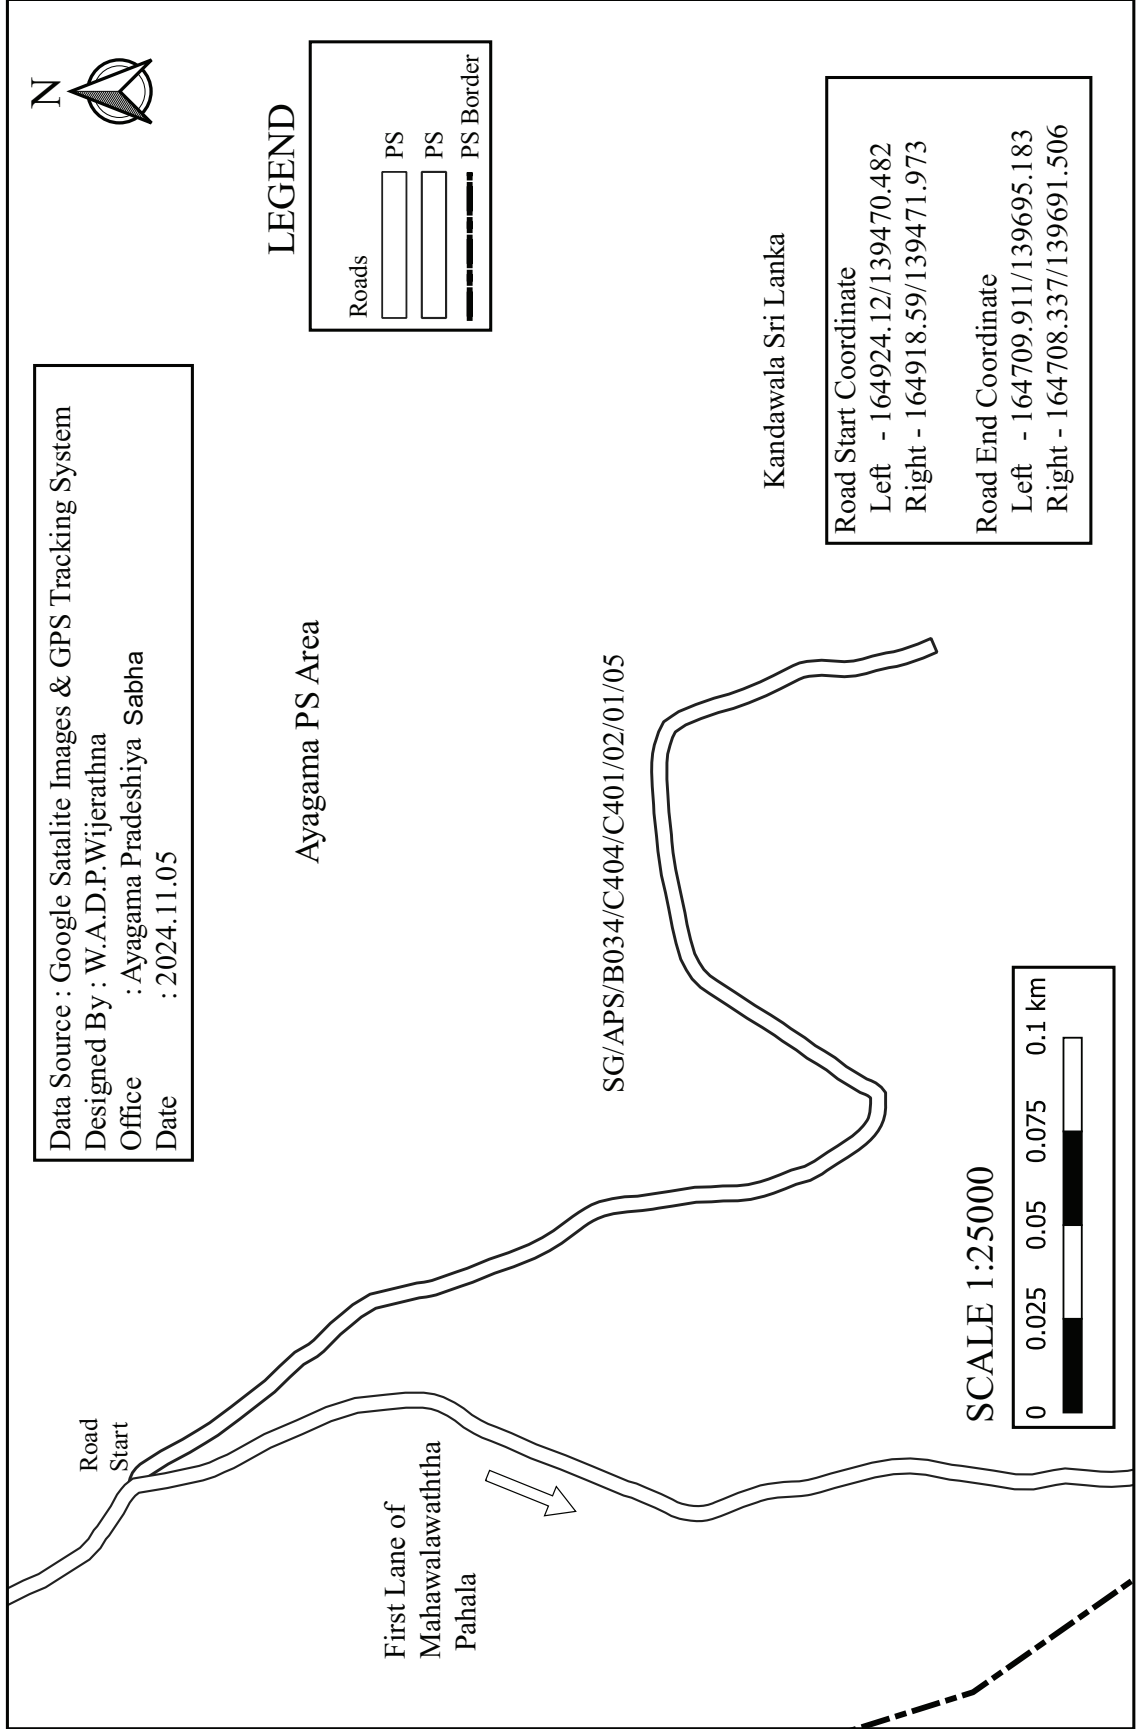

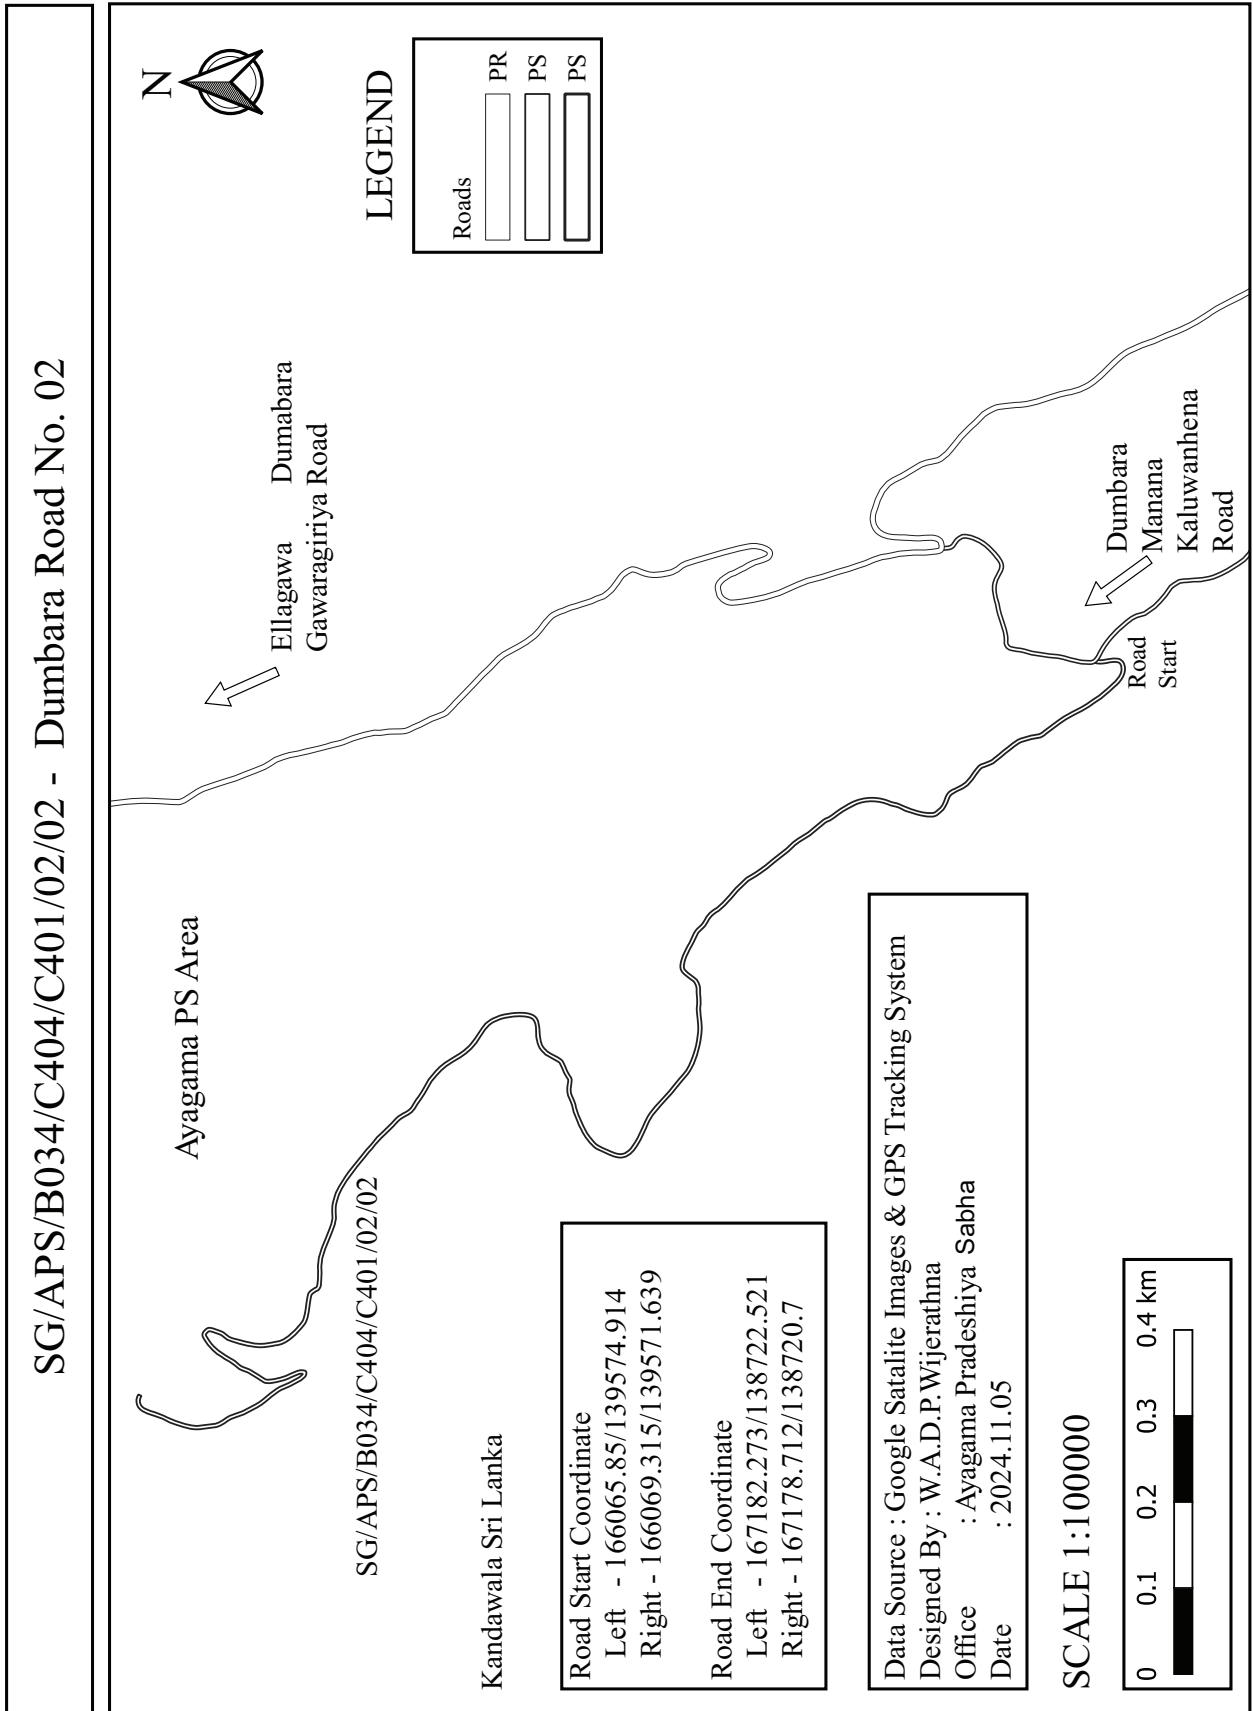

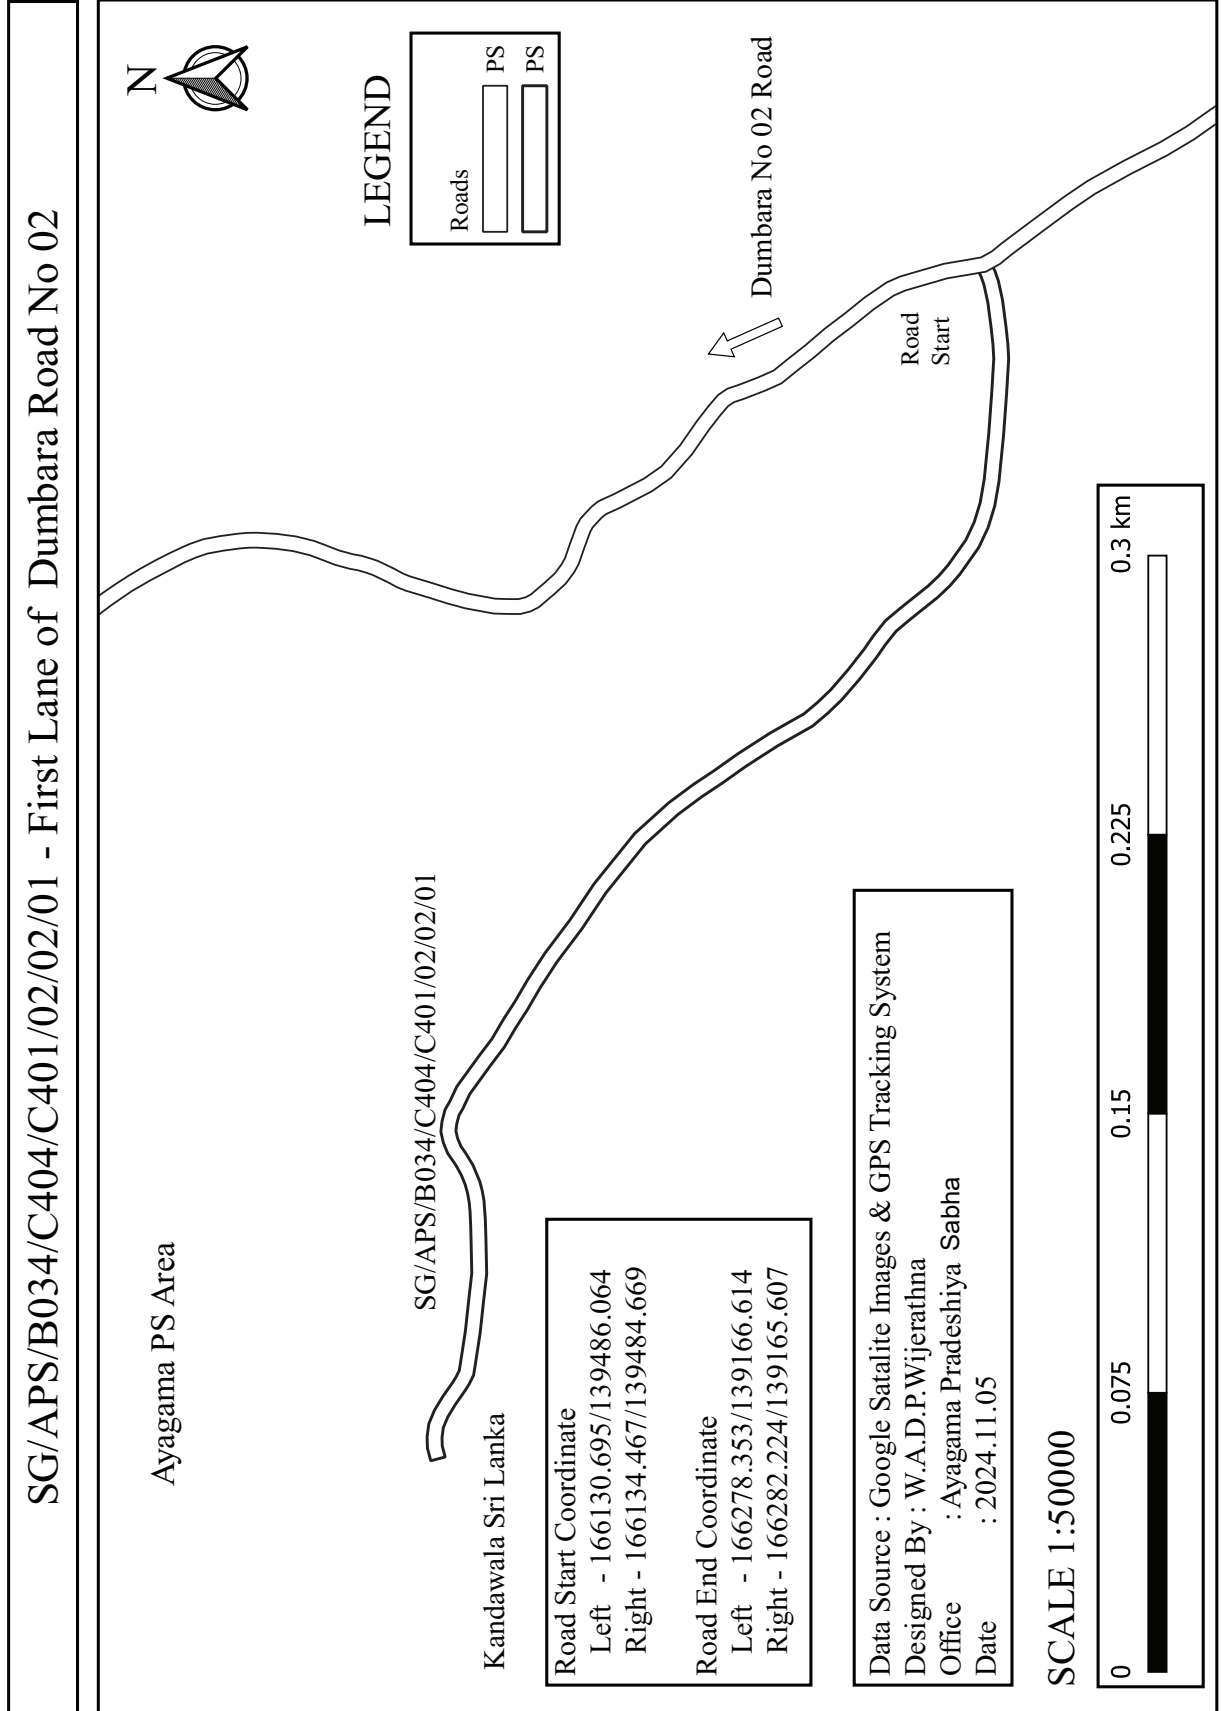

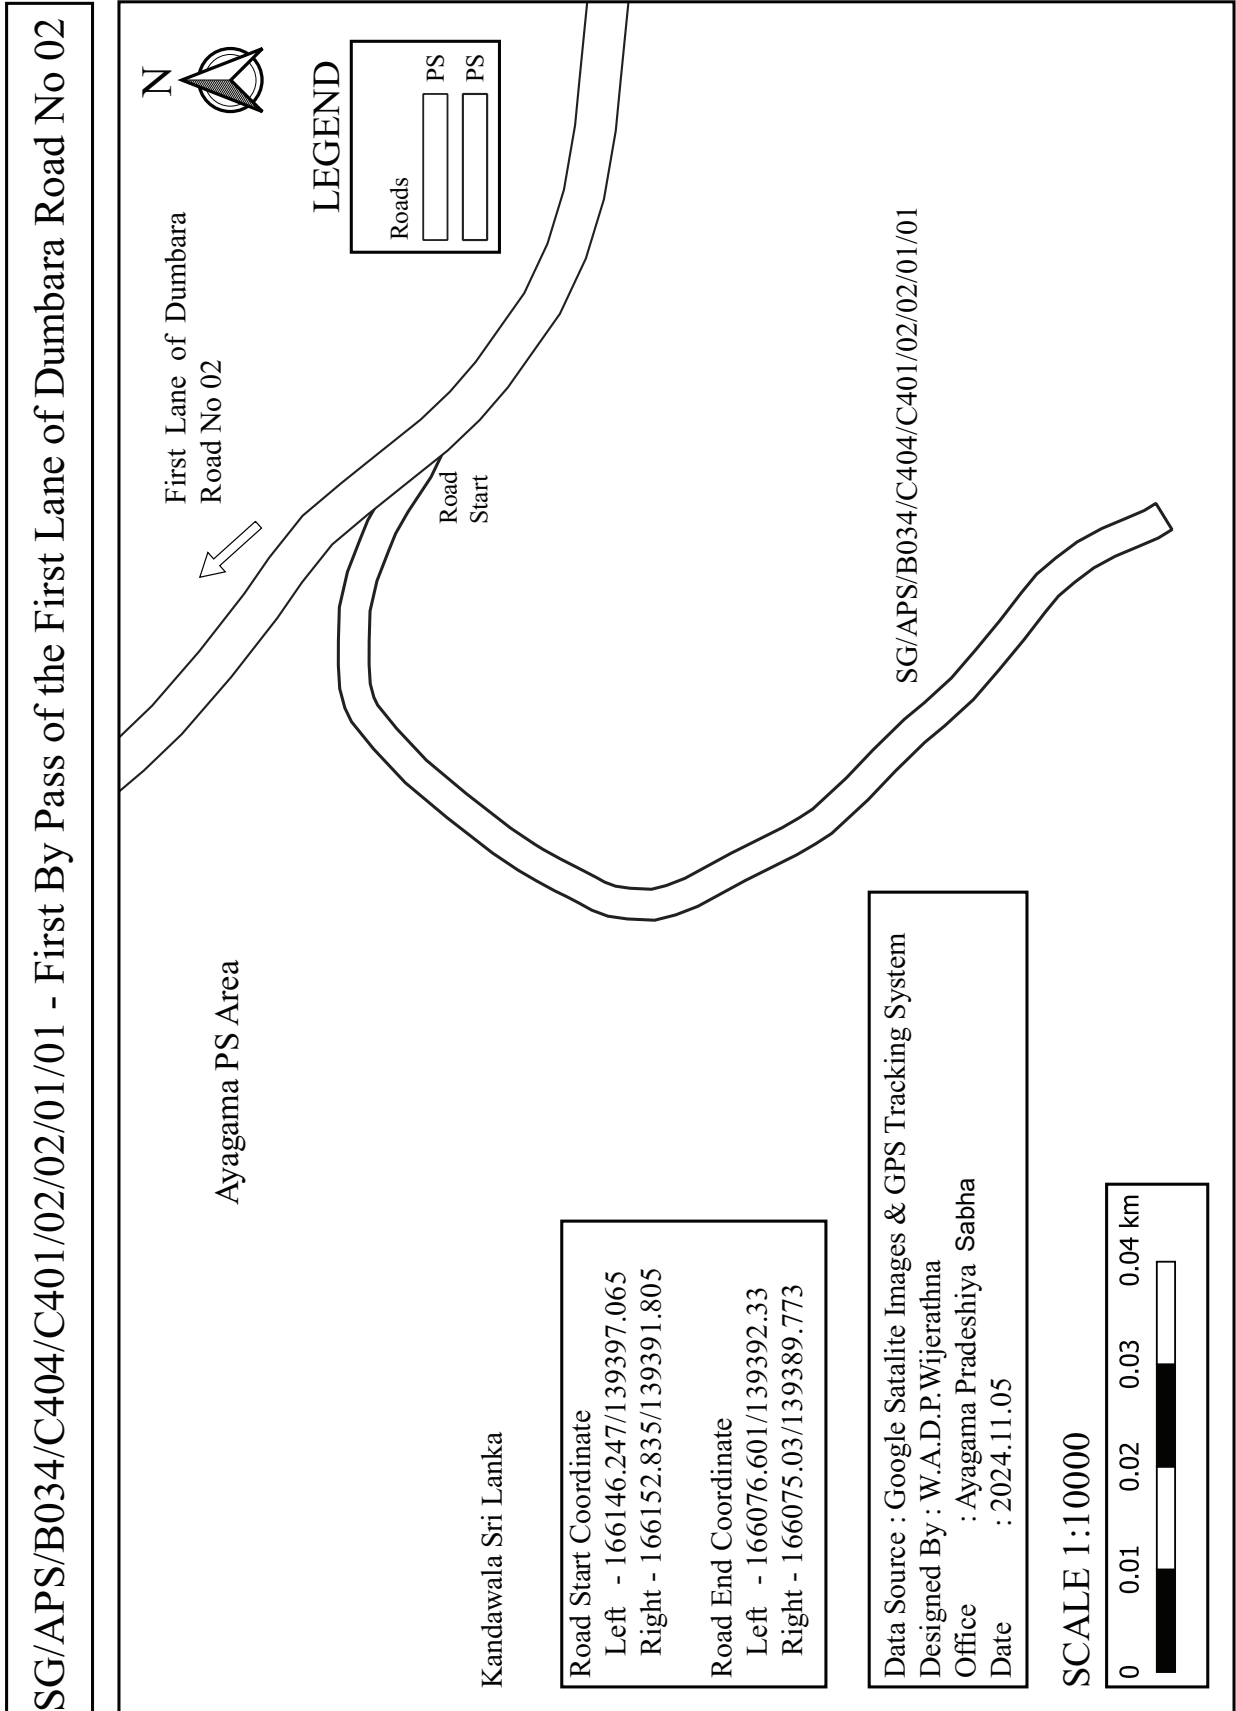

SG/APS/B034/C404/C401/03 - Dumbara Manana Kuttikanda Road



LEGEND

Roads

PR

PS

Data Source : Google Satalite Images & GPS Tracking System
 Designed By : W.A.D.P.Wijerathna
 Office : Ayagama Pradeshiya Sabha
 Date : 2024.11.05 Ayagama PS Area

SG/APS/B034/C404/C401/03

Kandawala Sri Lanka

Road Start Coordinate

Left - 164164.67/141345.967

Right - 164158.941/141346.65


Road End Coordinate


Left - 165891.23/142114.353


Right - 165896.228/142114.522


SCALE 1:250000


0 0.25 0.5 0.75 1 km

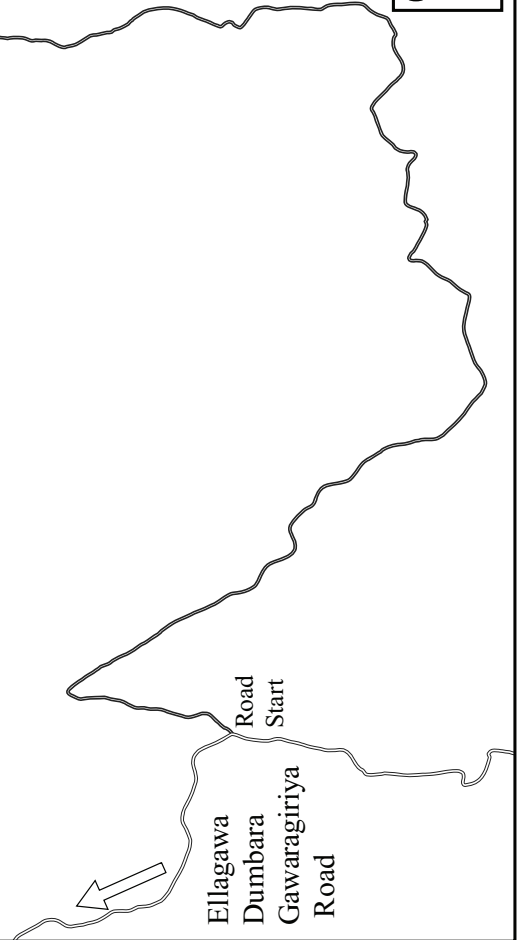

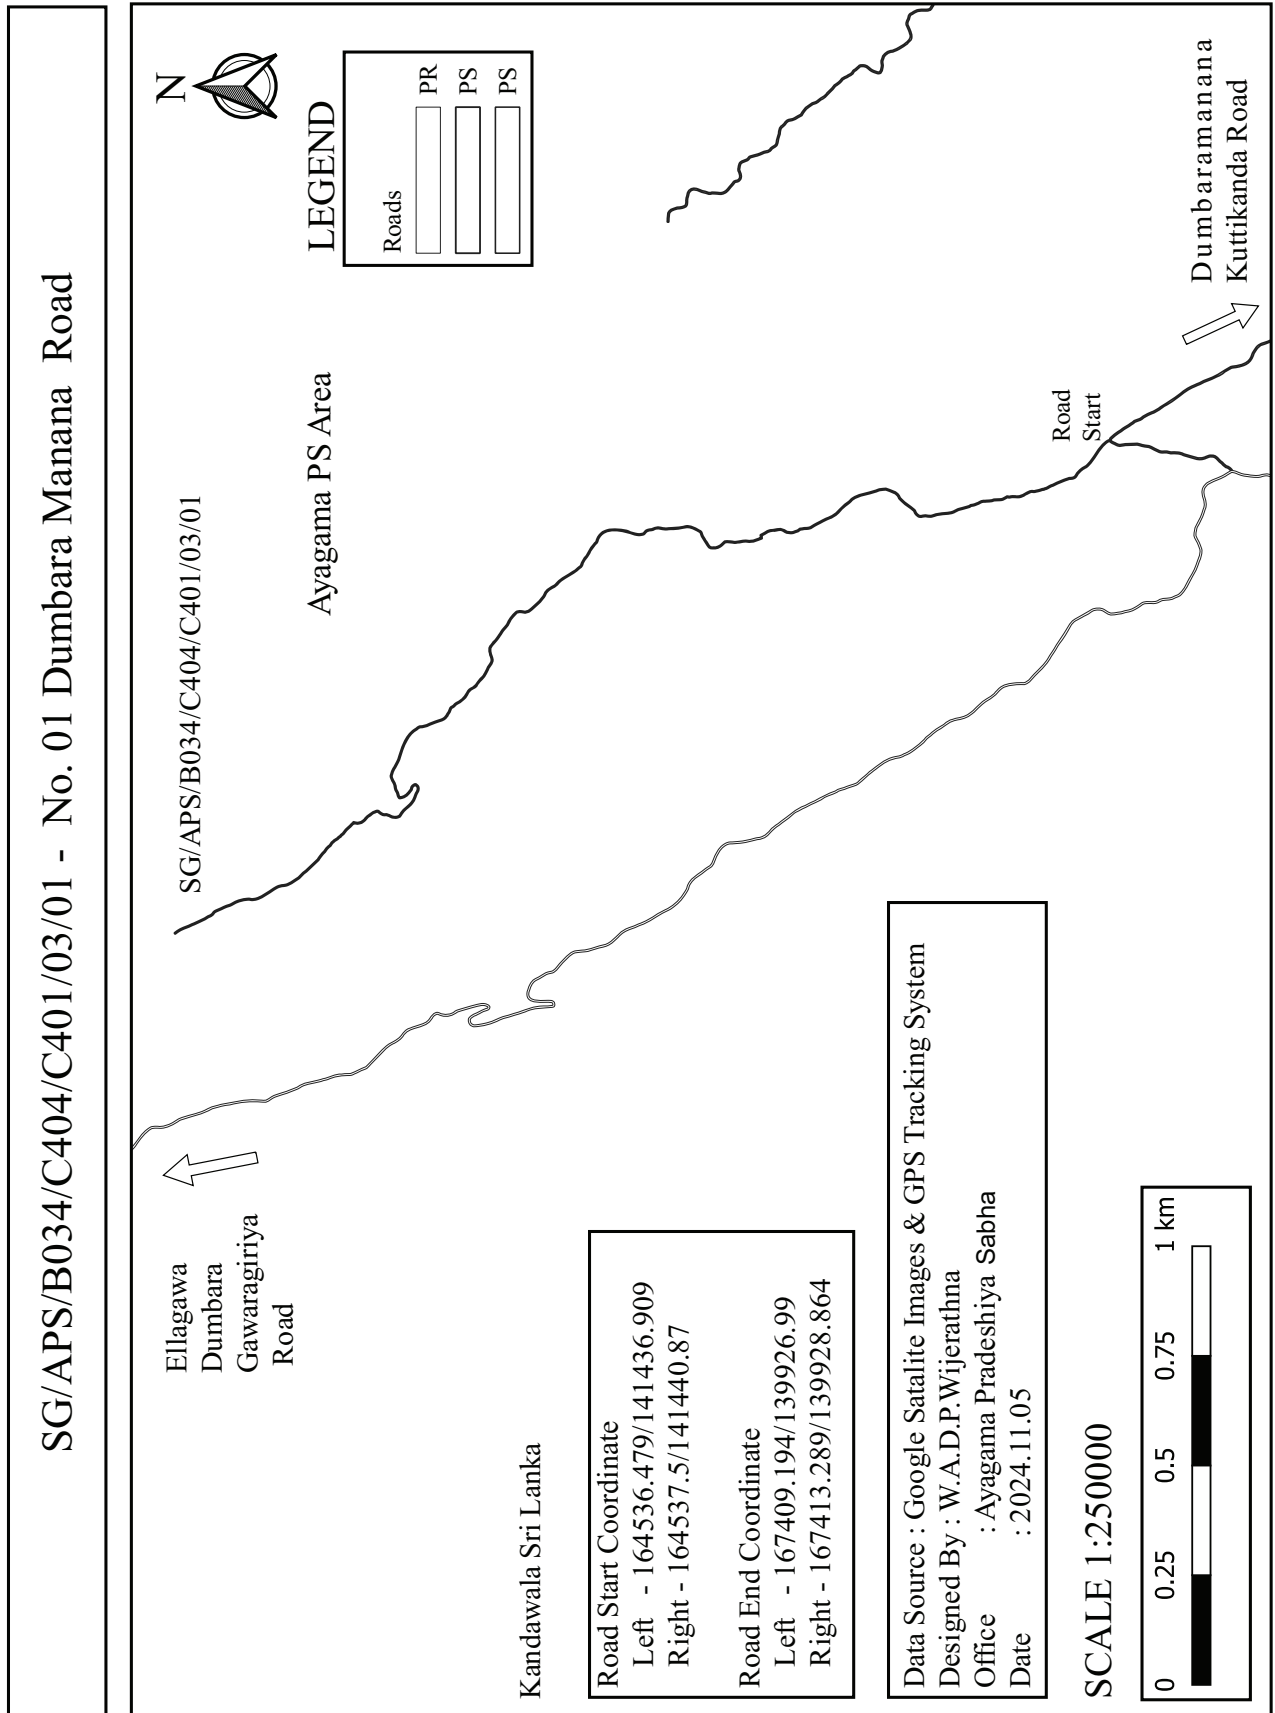

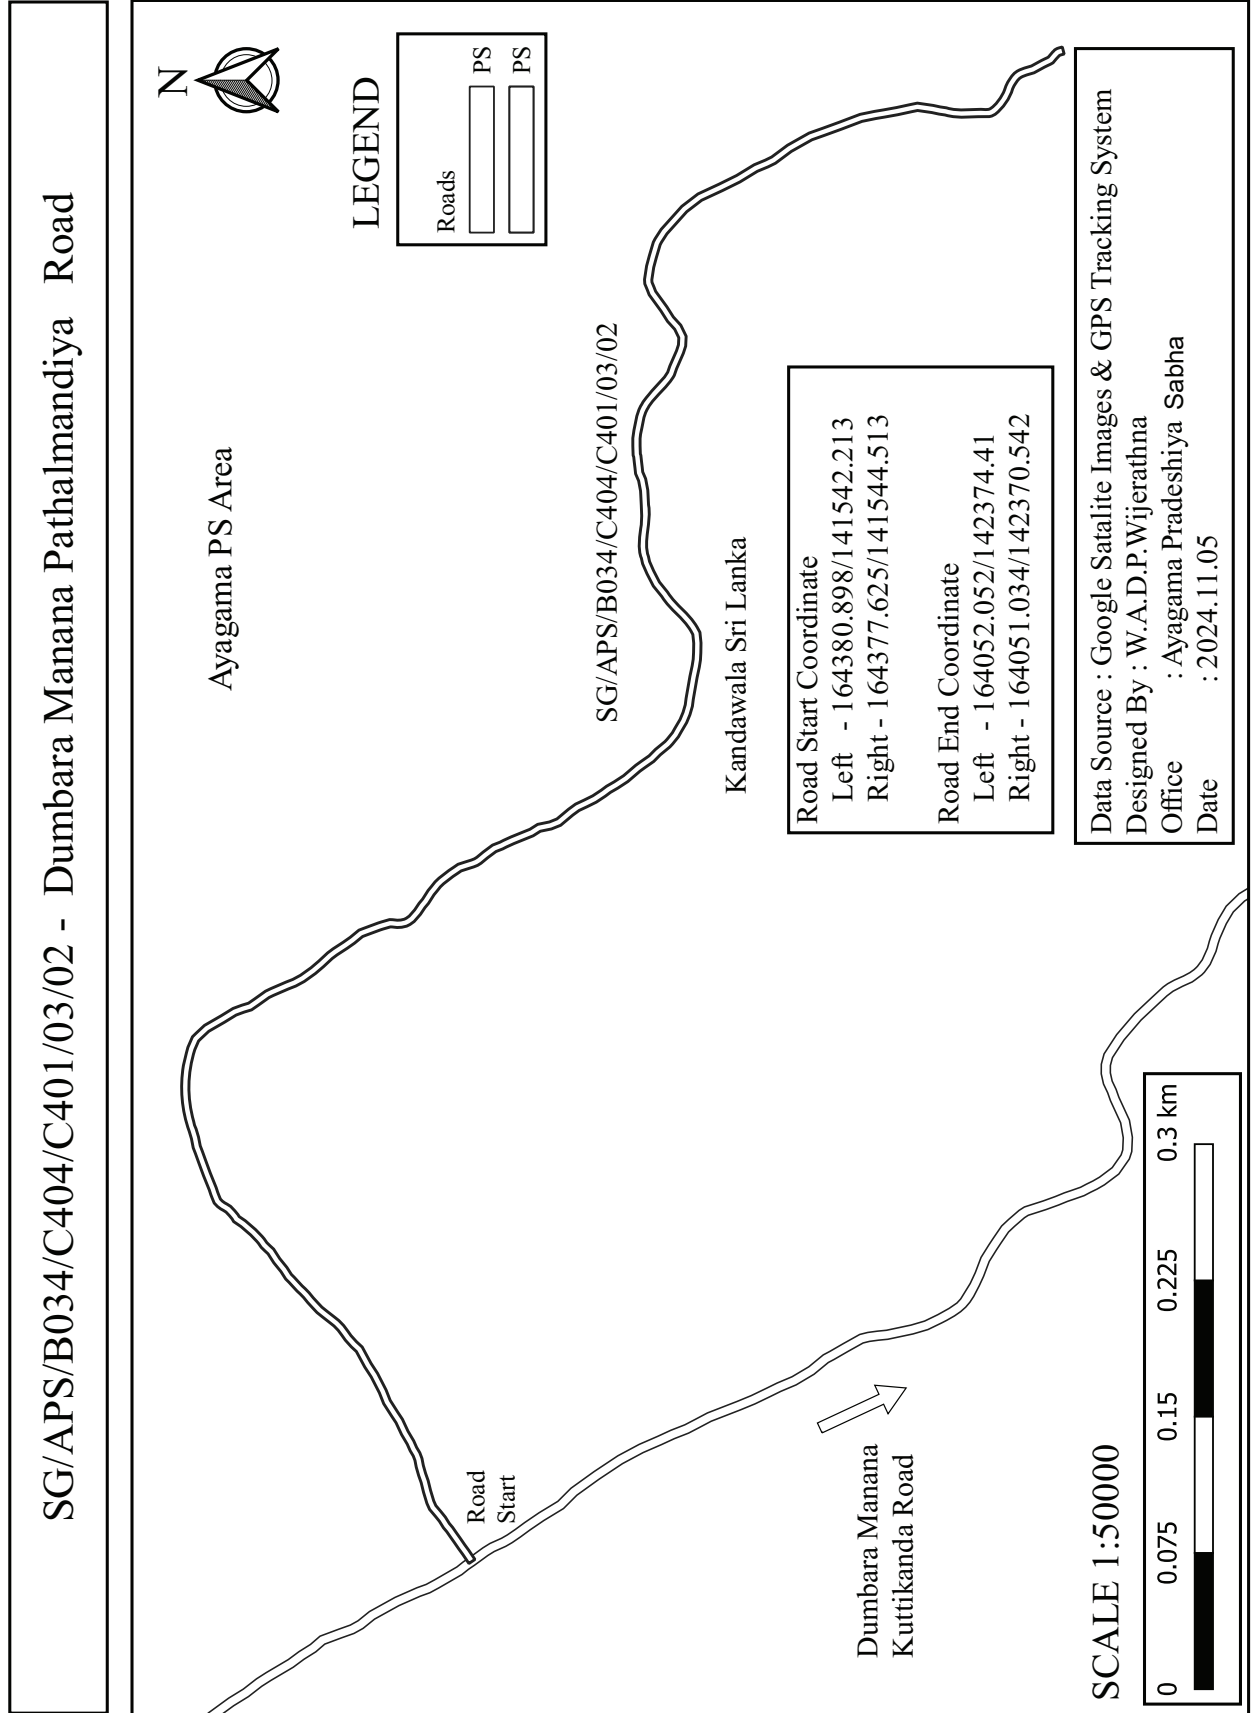

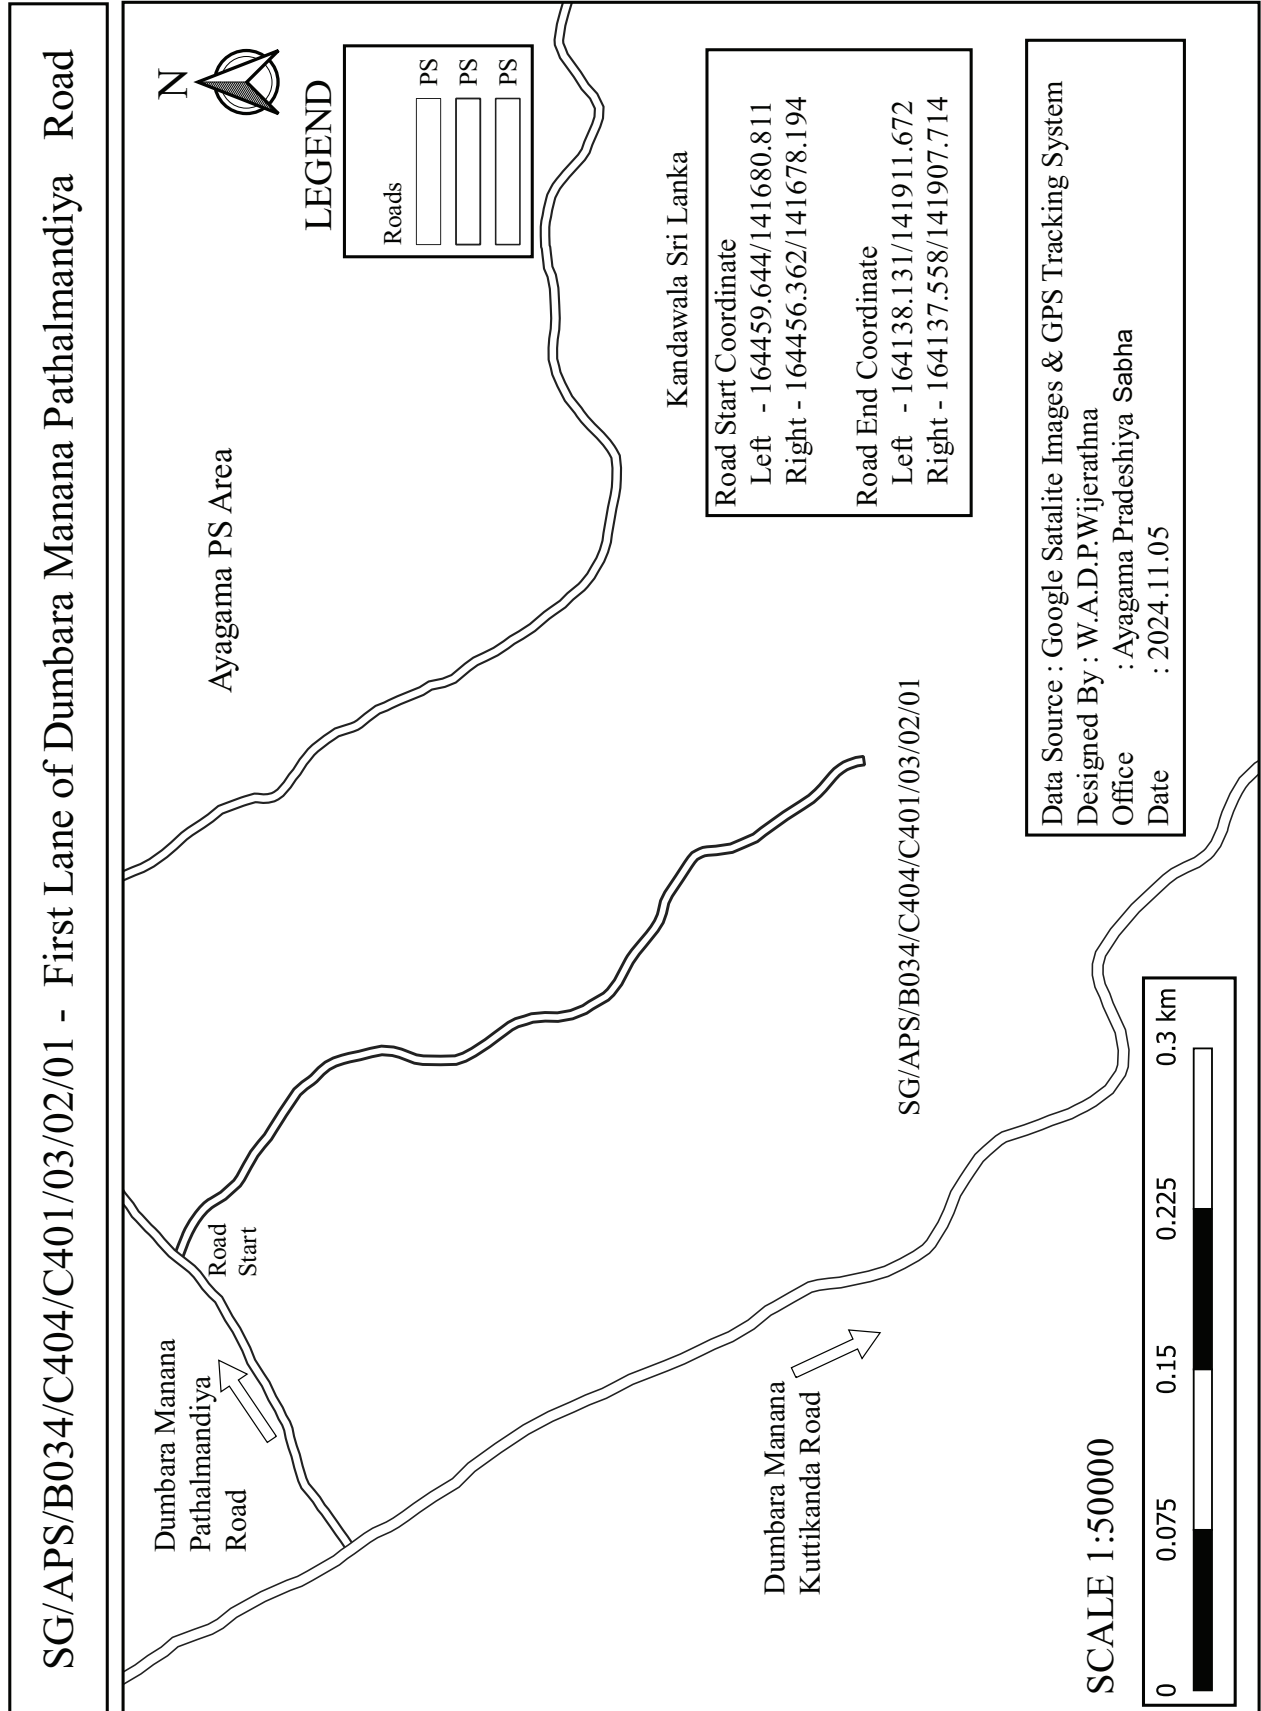

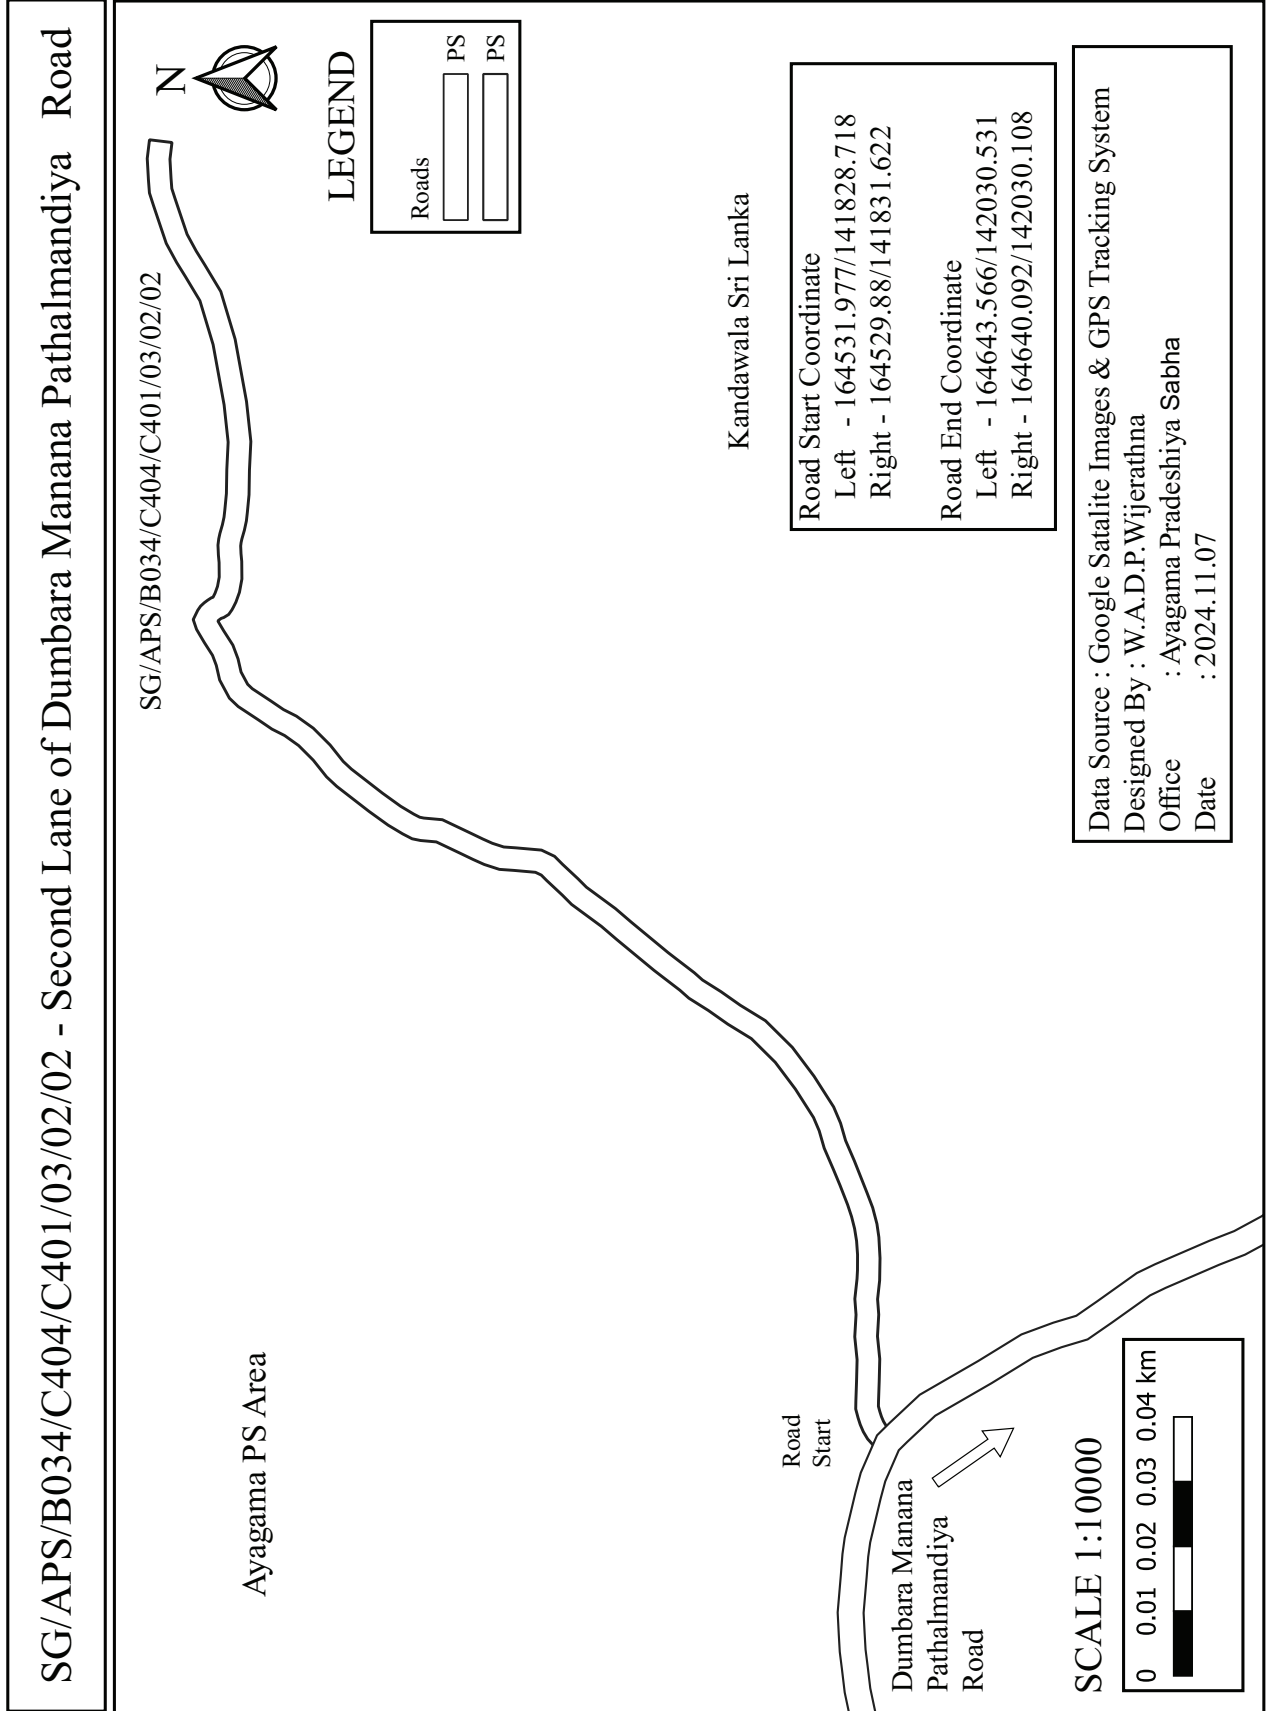

SG/APS/B034/C404/C401/03/02/02/01 - Dumbara Manana Miyangala Kurunda Road



LEGEND

Roads



SG/APS/B034/C404/C401/03/02/02/01

Ayagama PS Area

Kandawala Sri Lanka

Road Start Coordinate

Left - 164636.291/141954.722

Right - 164634.939/141959.151

Road End Coordinate

Left - 165198.71/141807.634

Right - 165202.07/141804.641

Data Source : Google Satalite Images & GPS Tracking System

Designed By : W.A.D.P.Wijerathna


Office : Ayagama Pradeshiya Sabha

Date : 2024.11.07


Road Start


Second Lane of Dumbara Manana Pathalmandiya Road


SCALE 1:25000

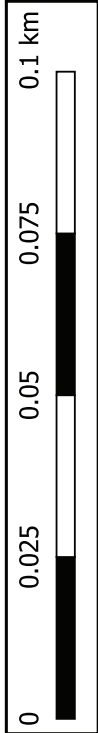



SG/APS/B034/C404/C401/03/02/03 - Third Lane of Dumbara Manana Pathalmandiya Road

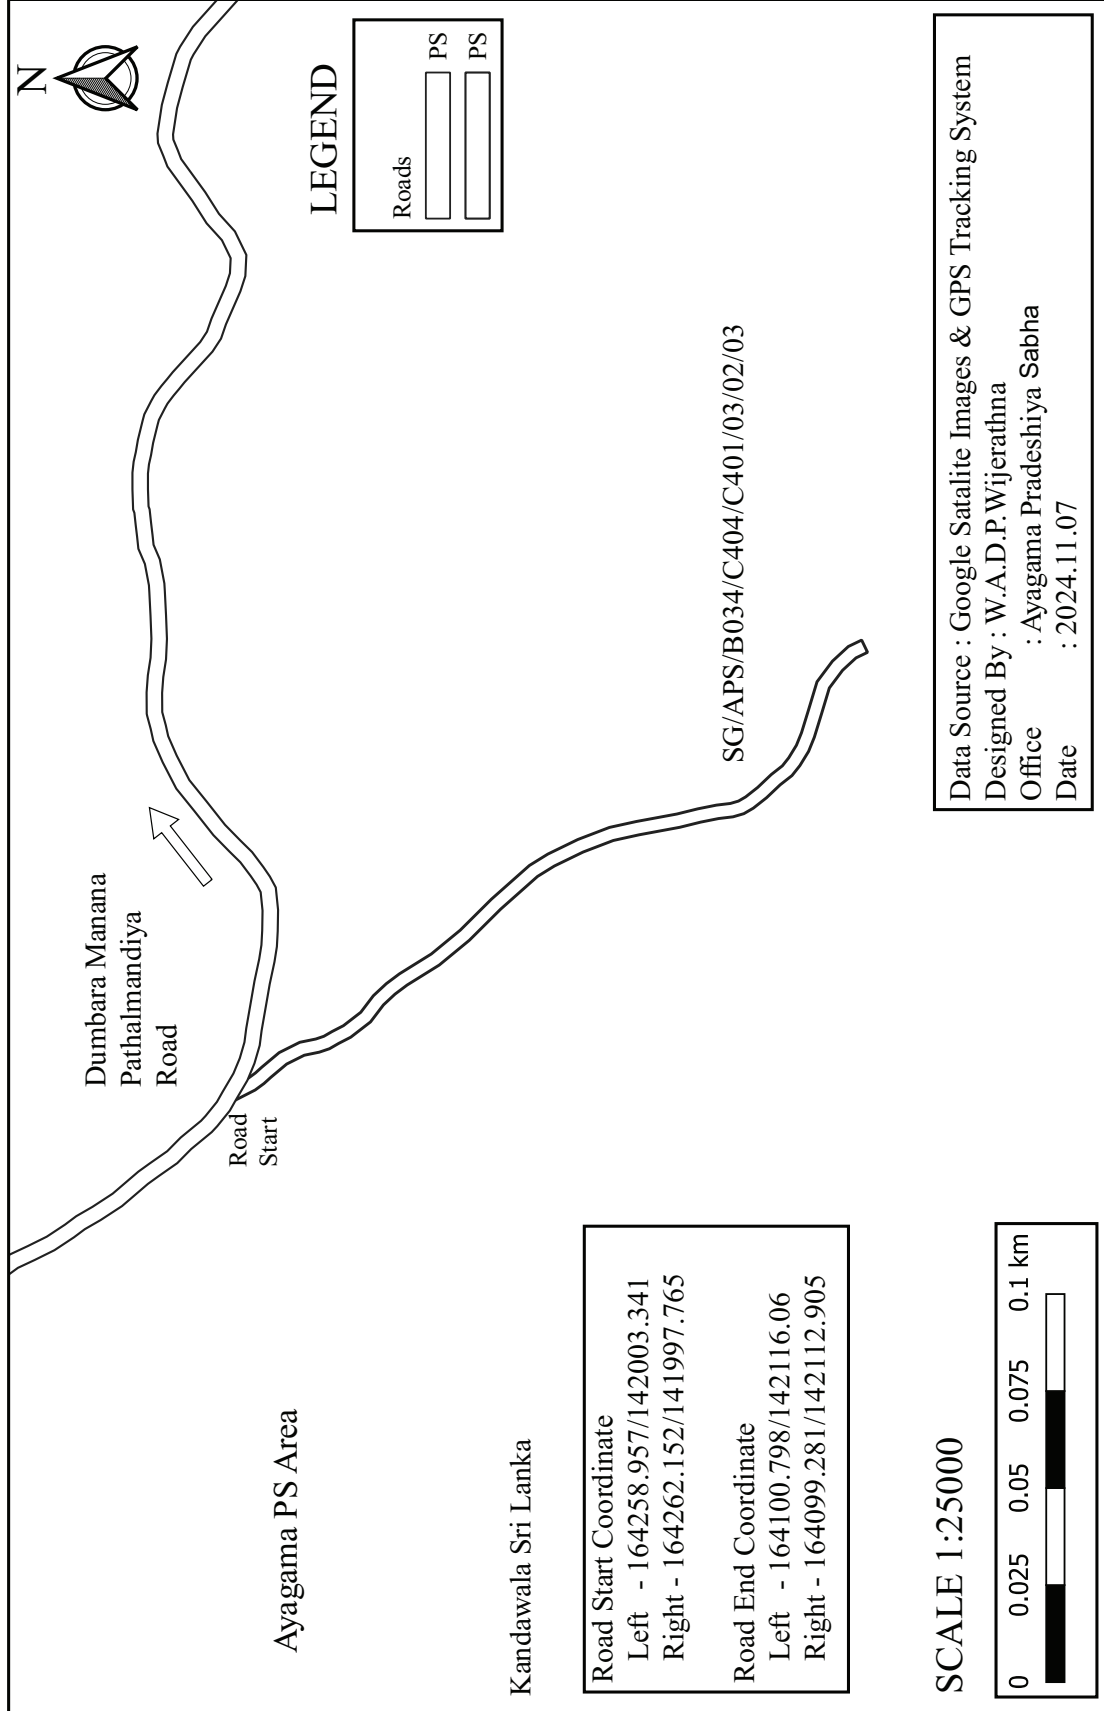

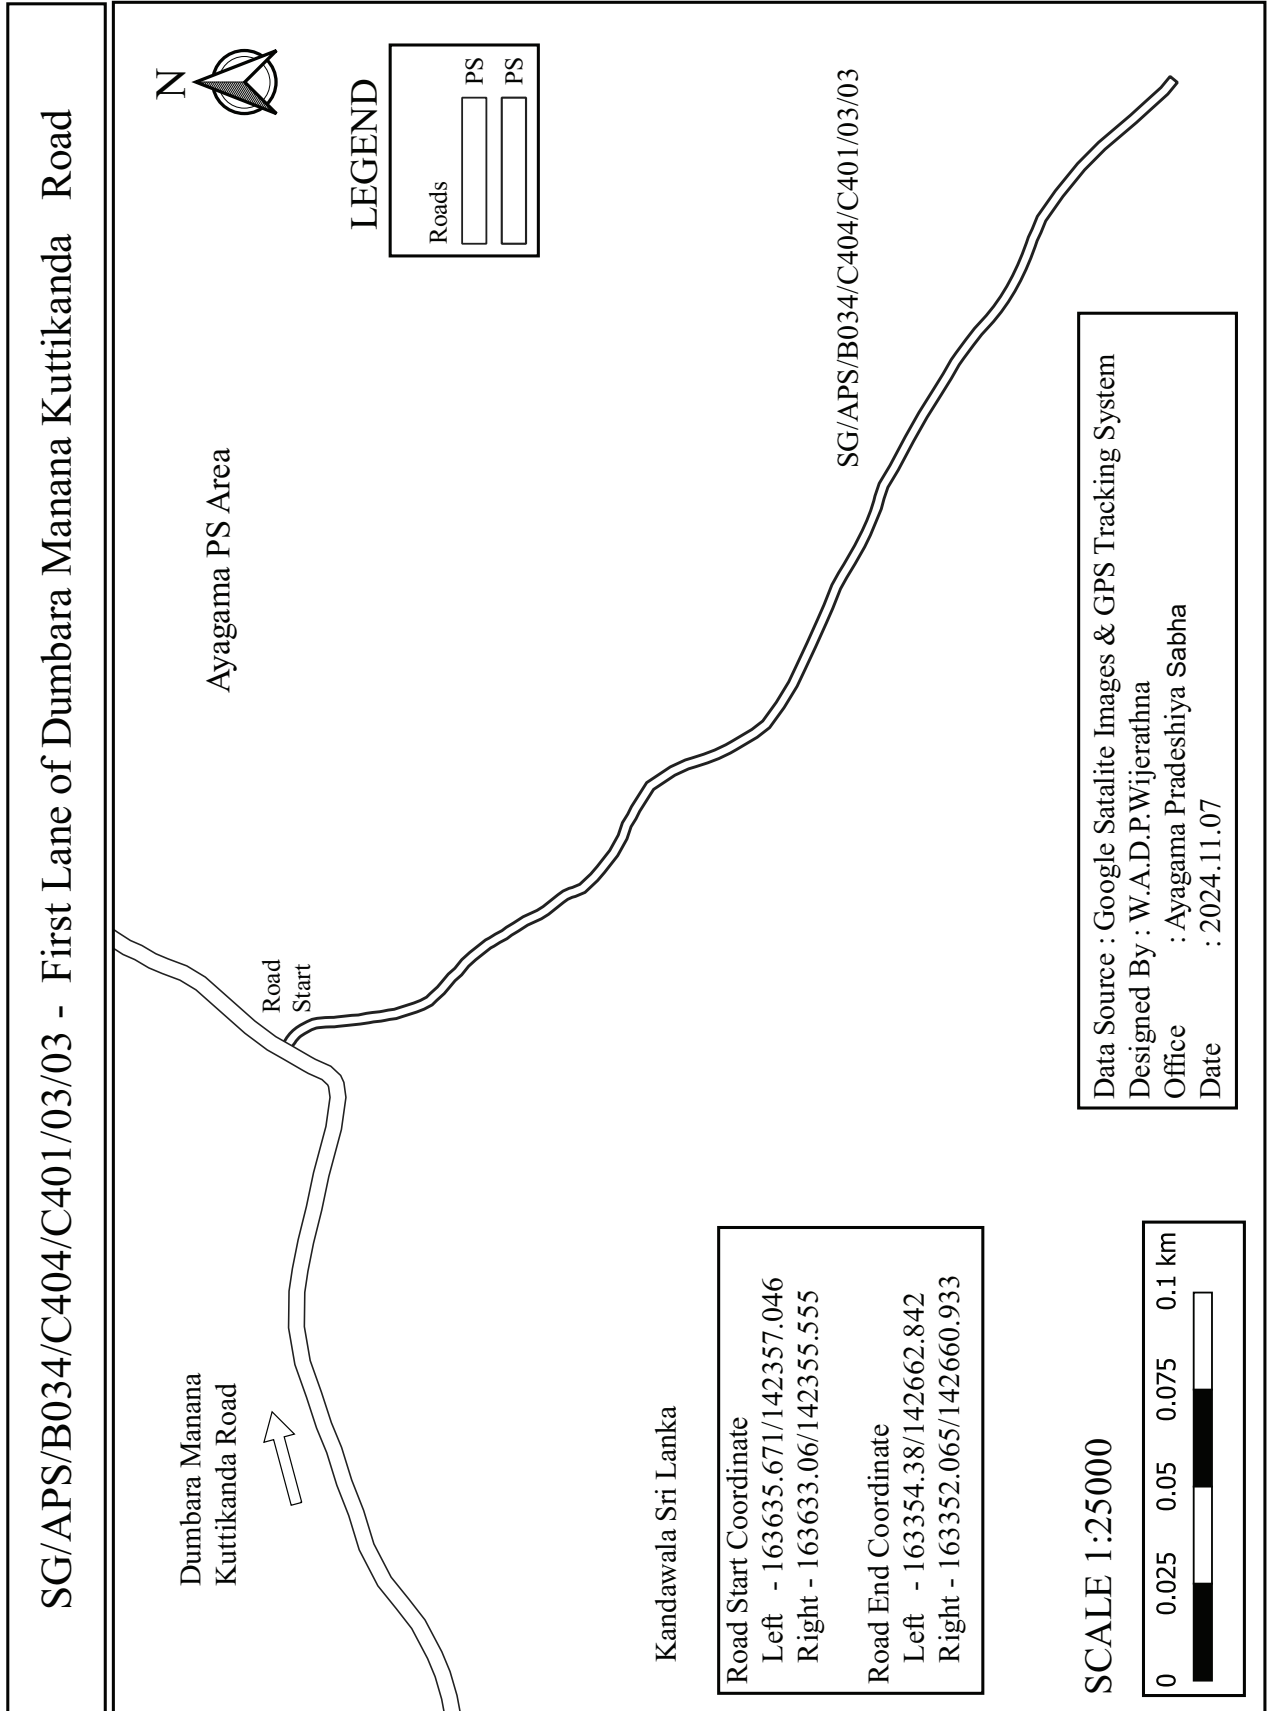


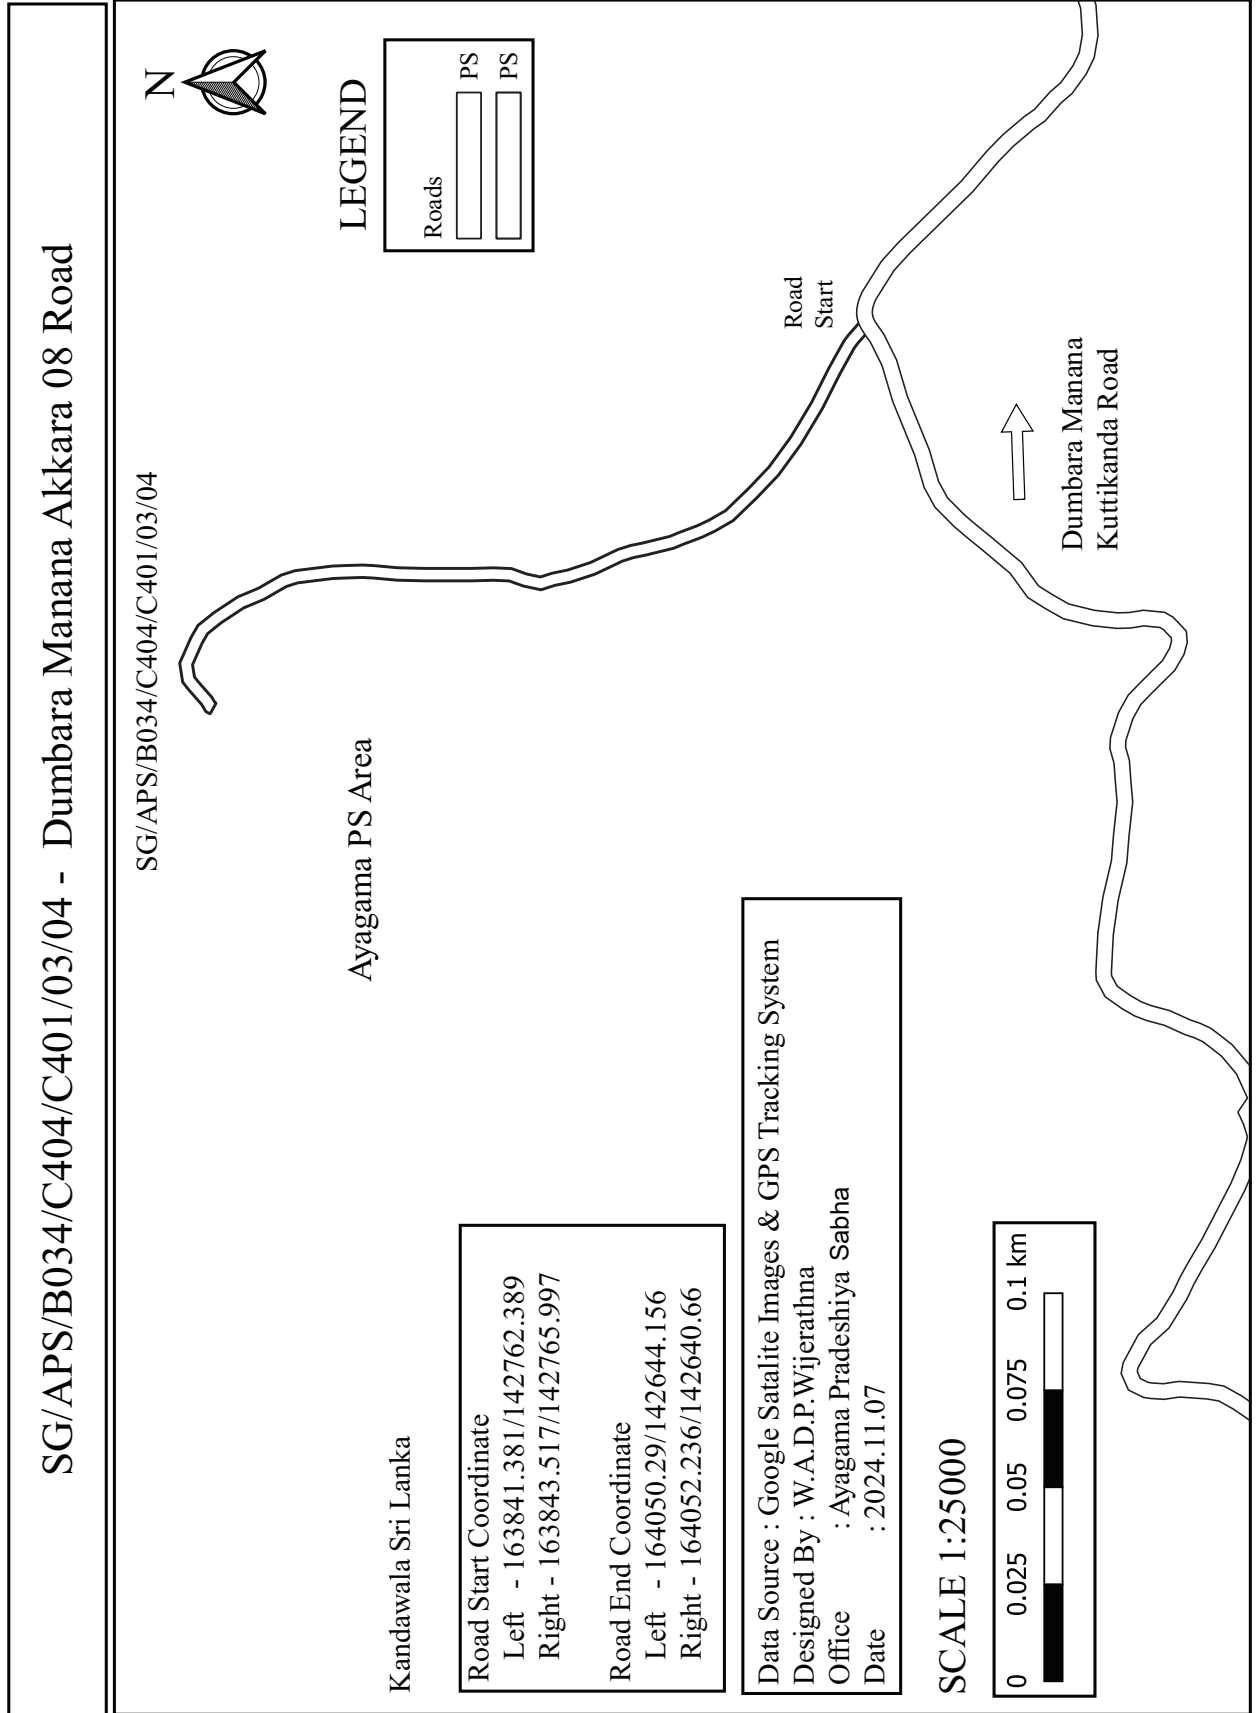


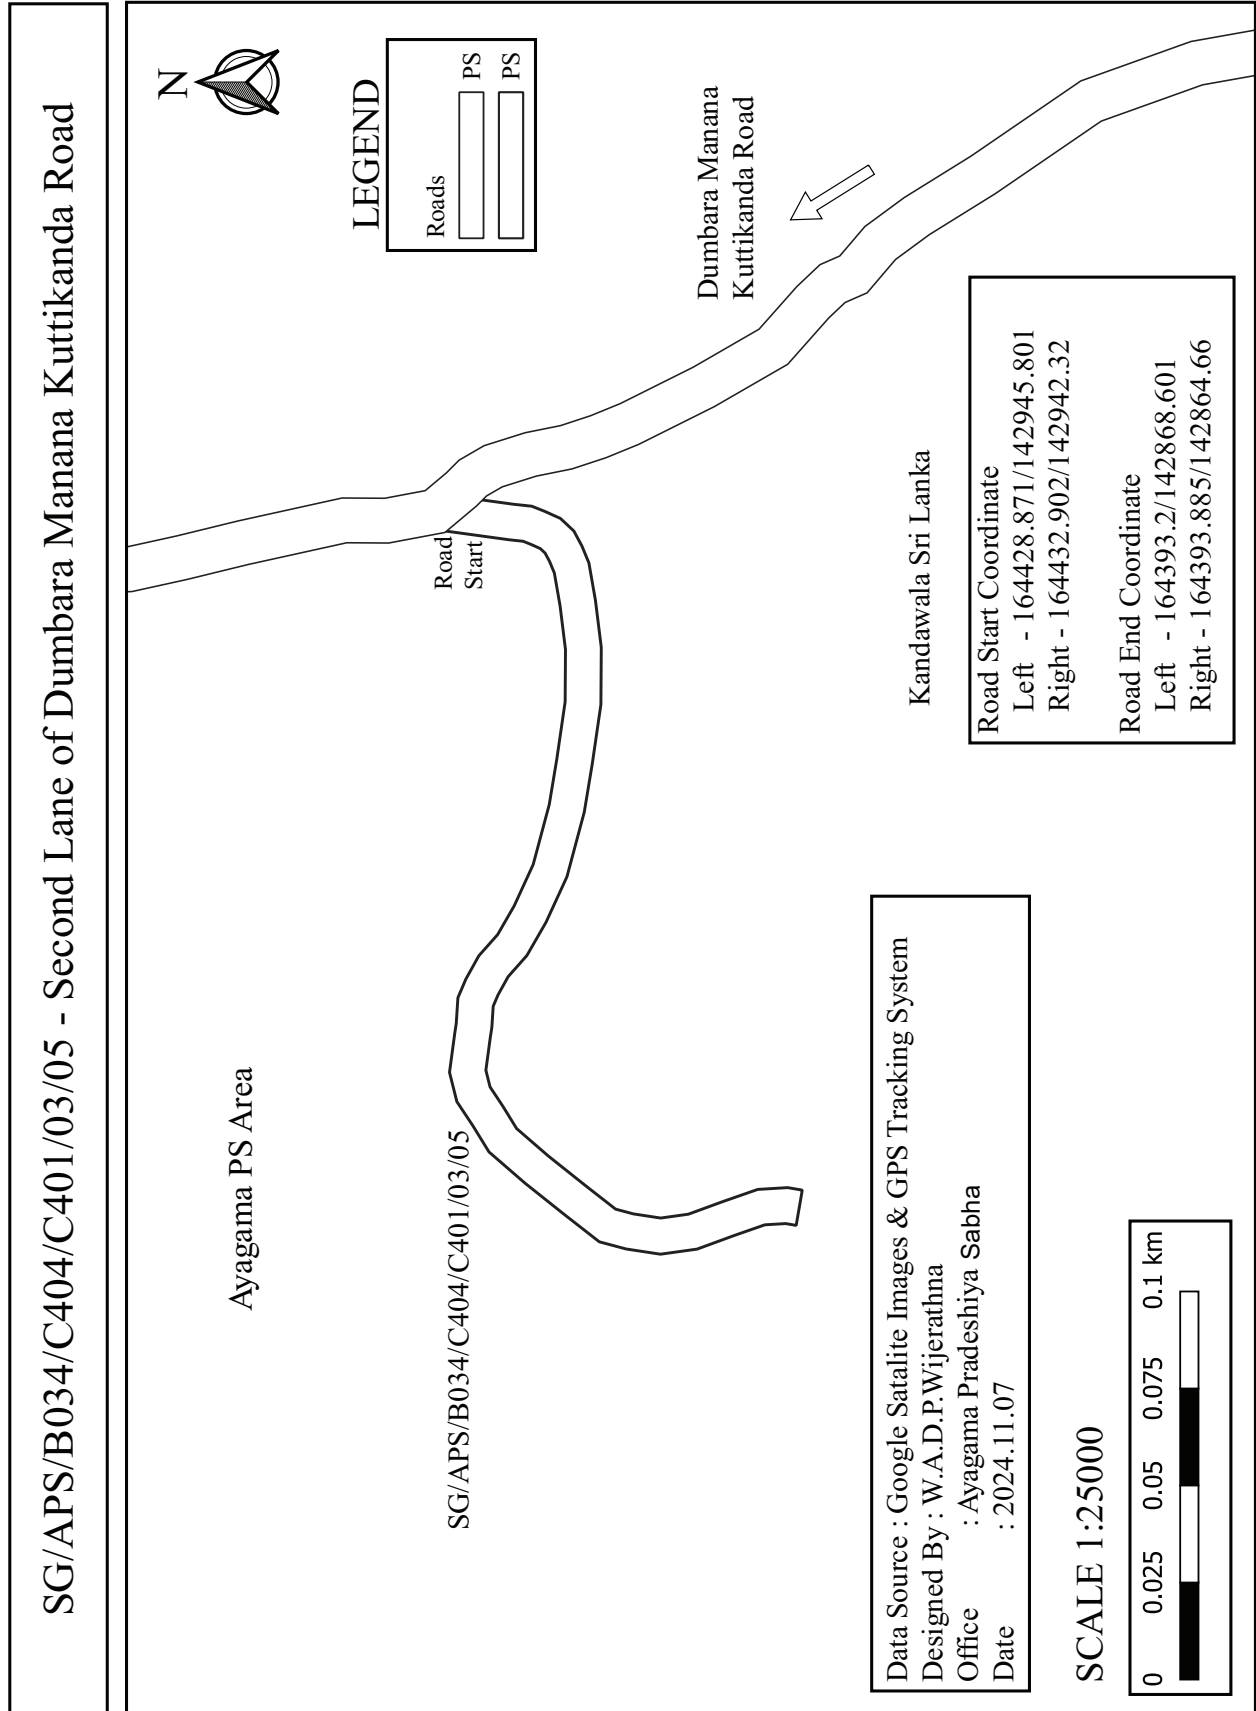

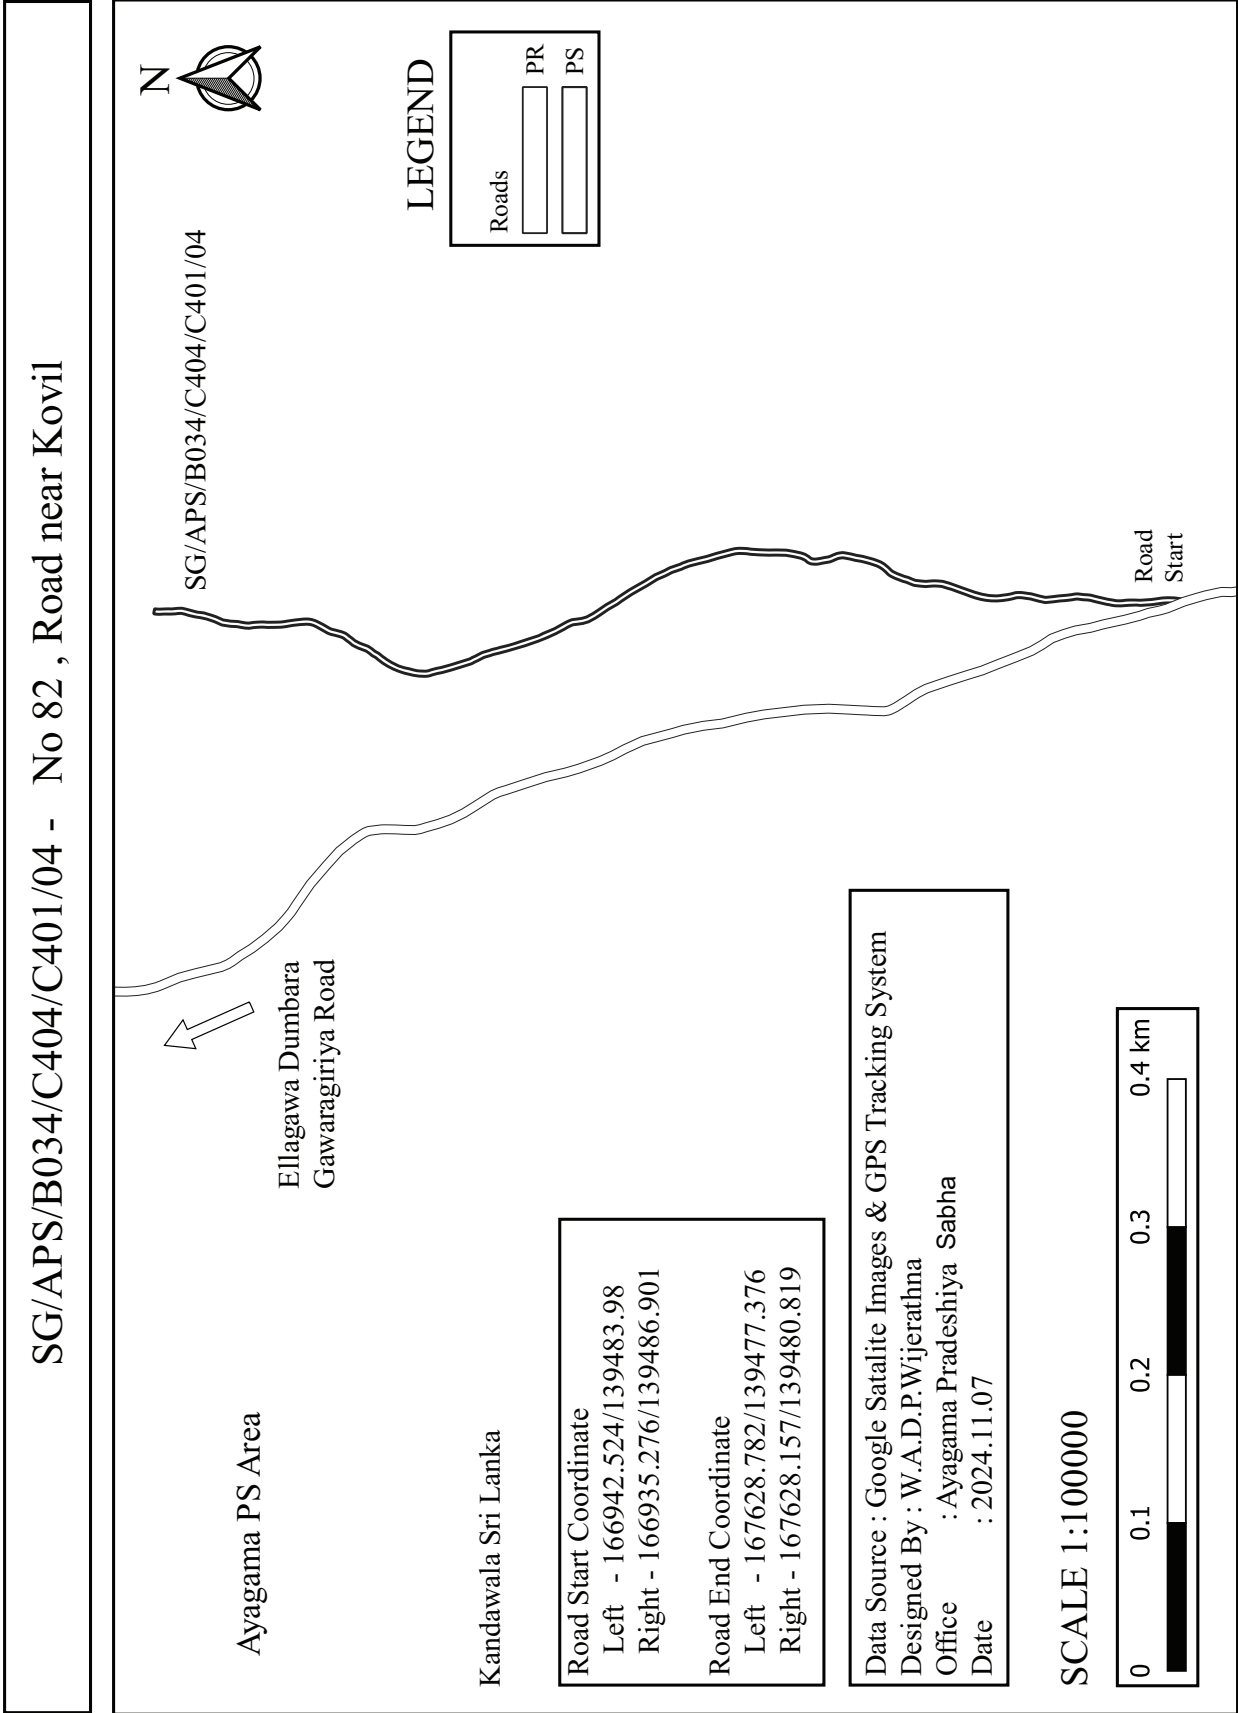



SG/APS/B034/C404/C401/05 - Footpath No.82 Dumbara

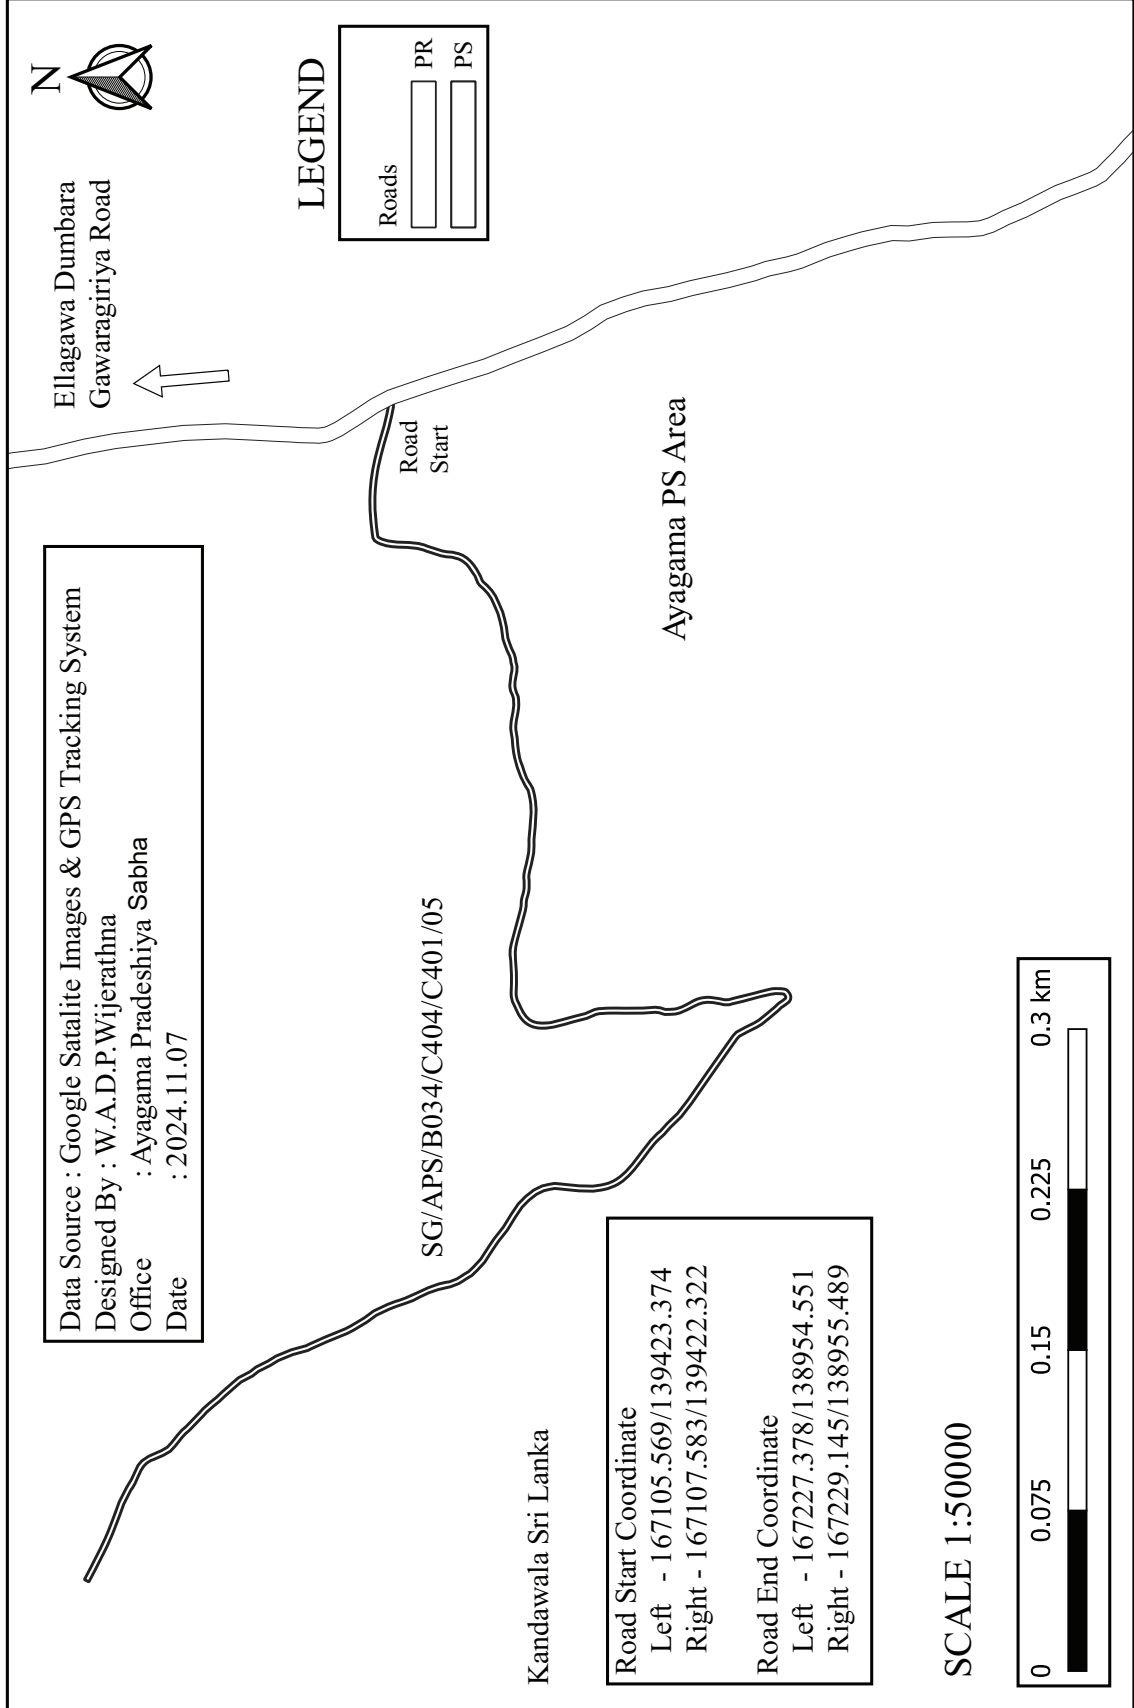

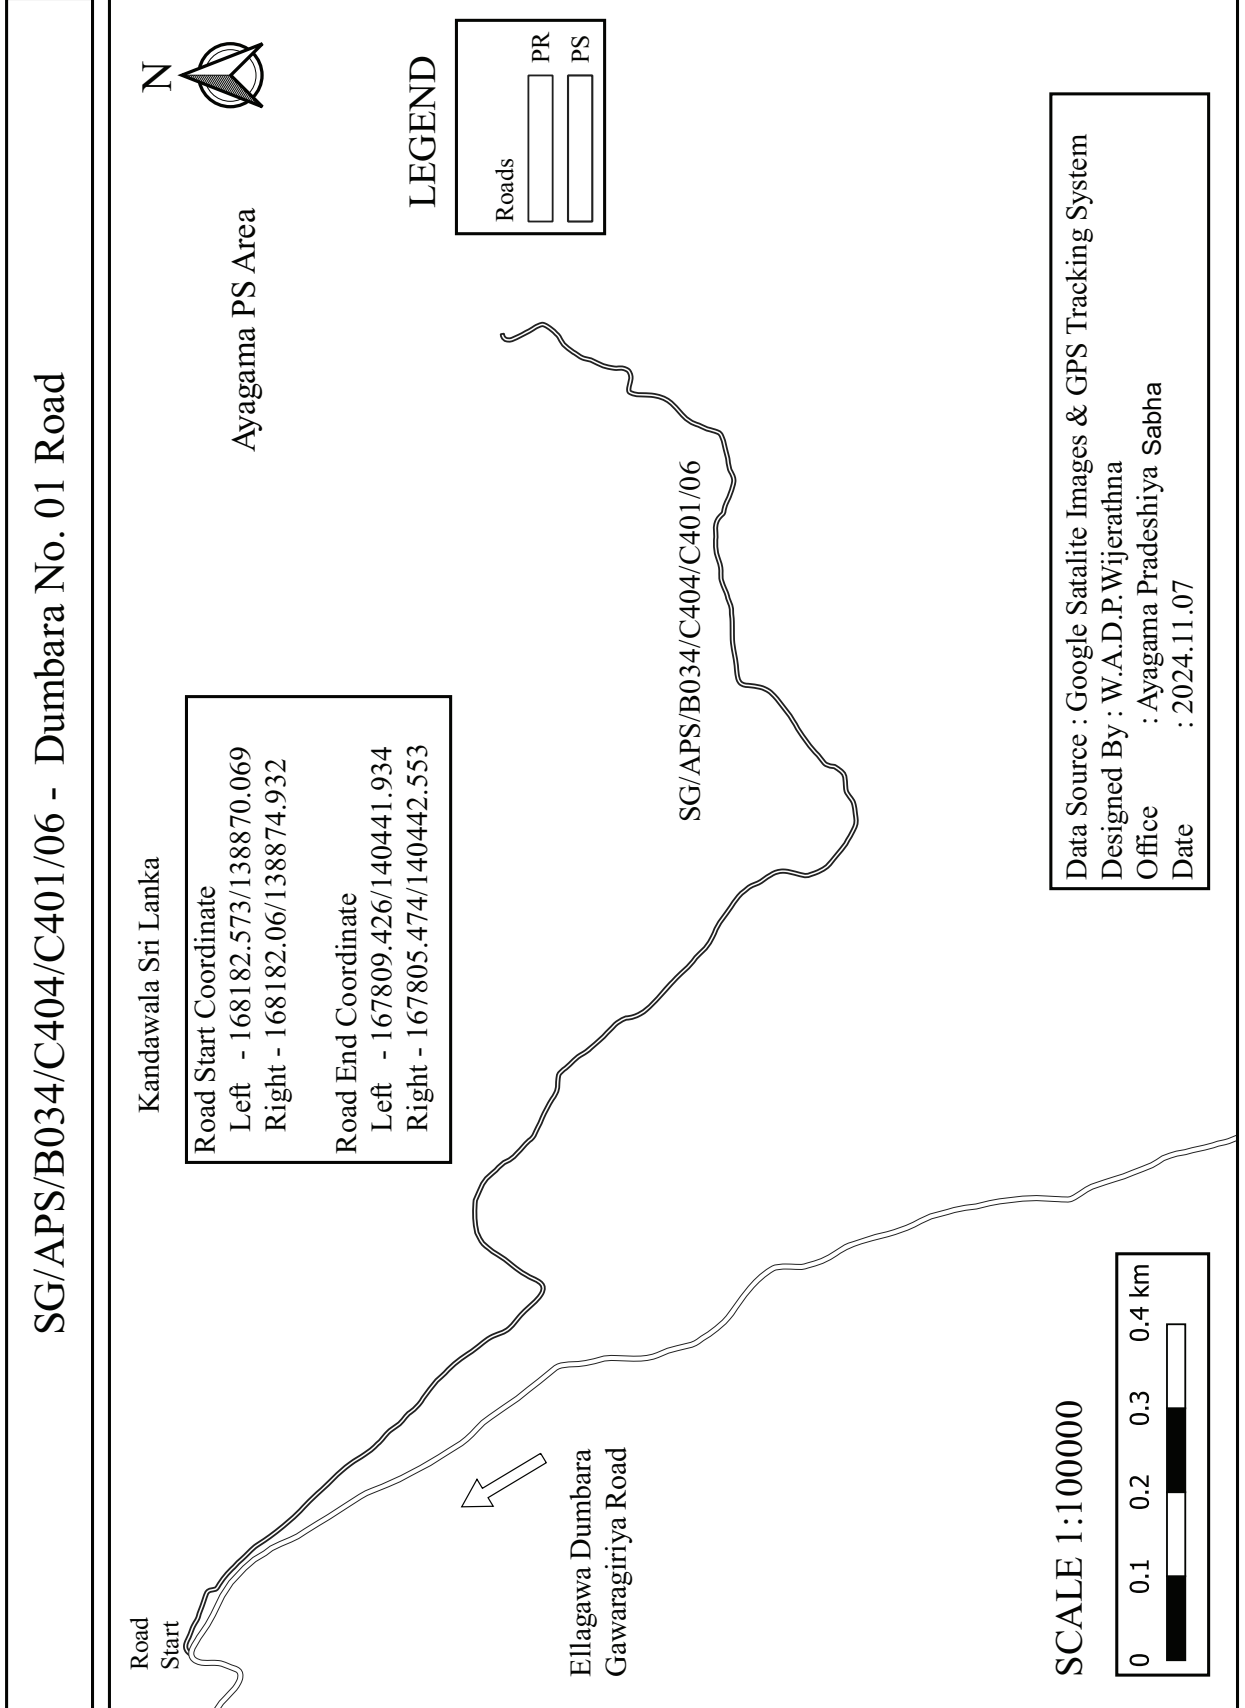



SG/APS/B034/C404/C401/07 - Dumbara Medikella Ihala Road

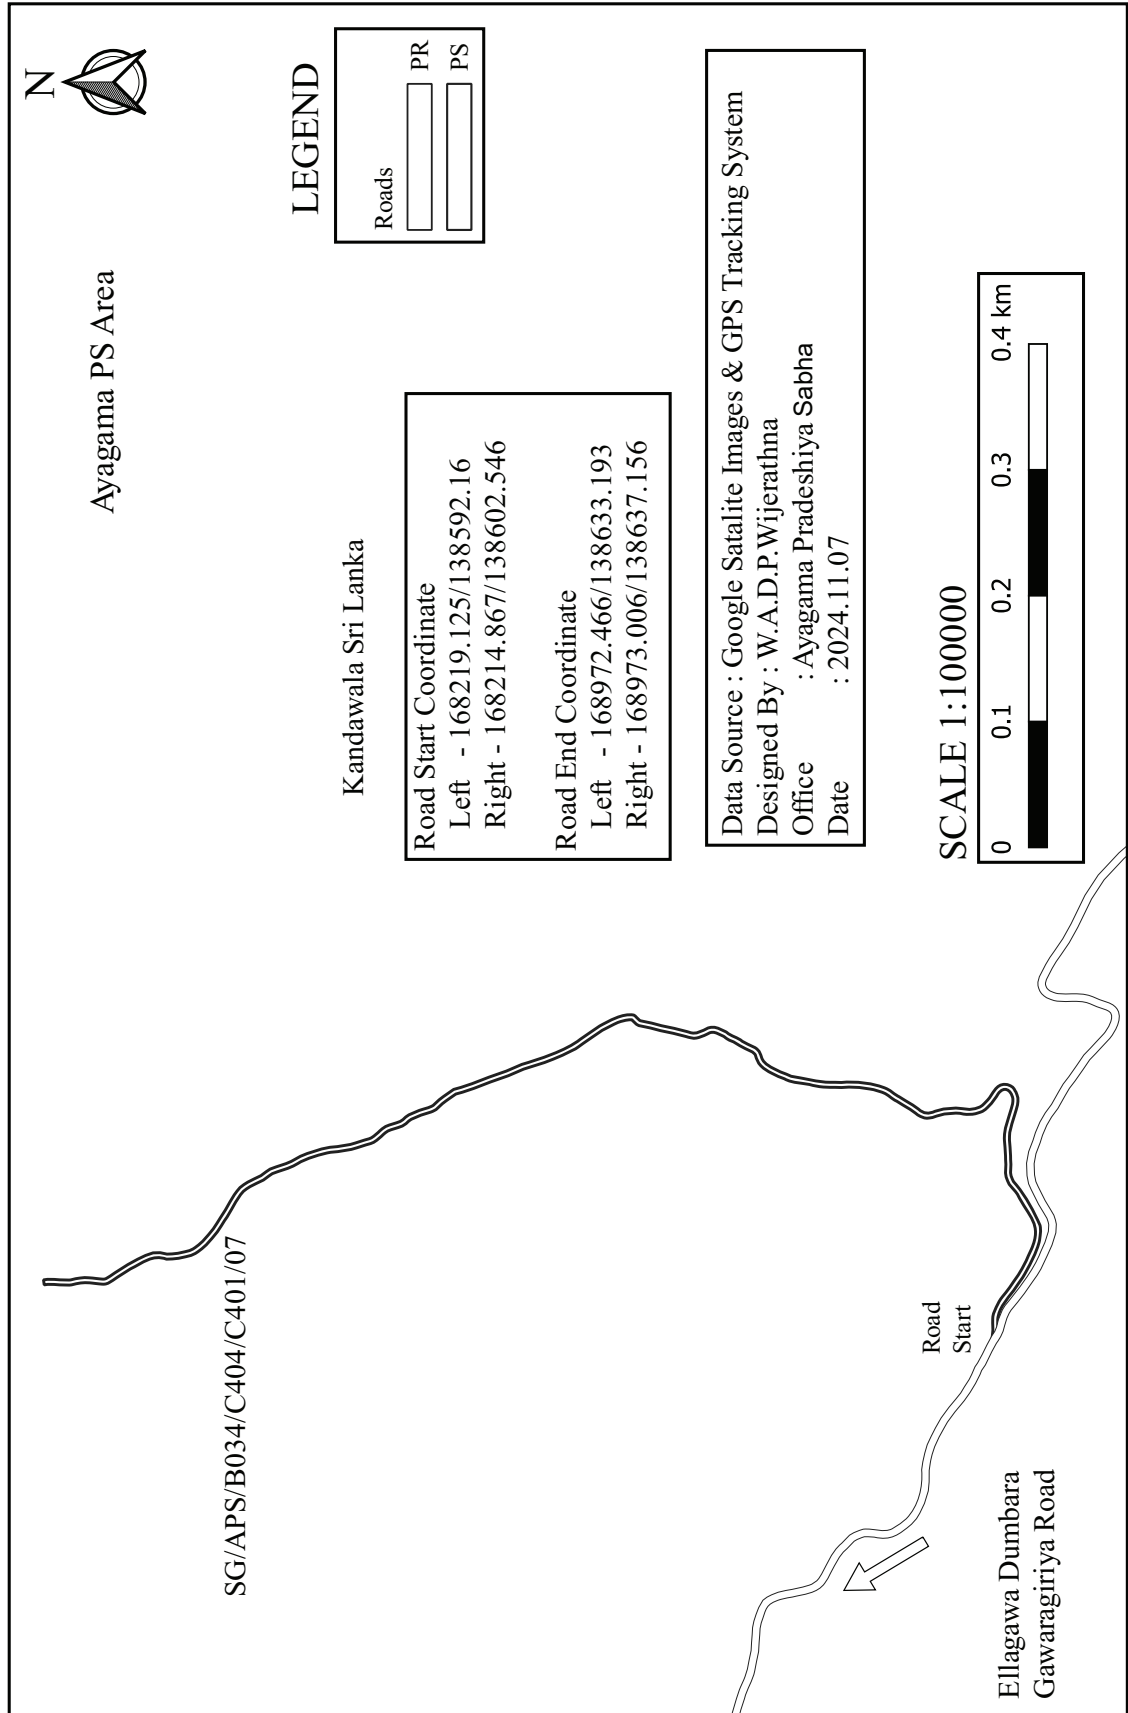


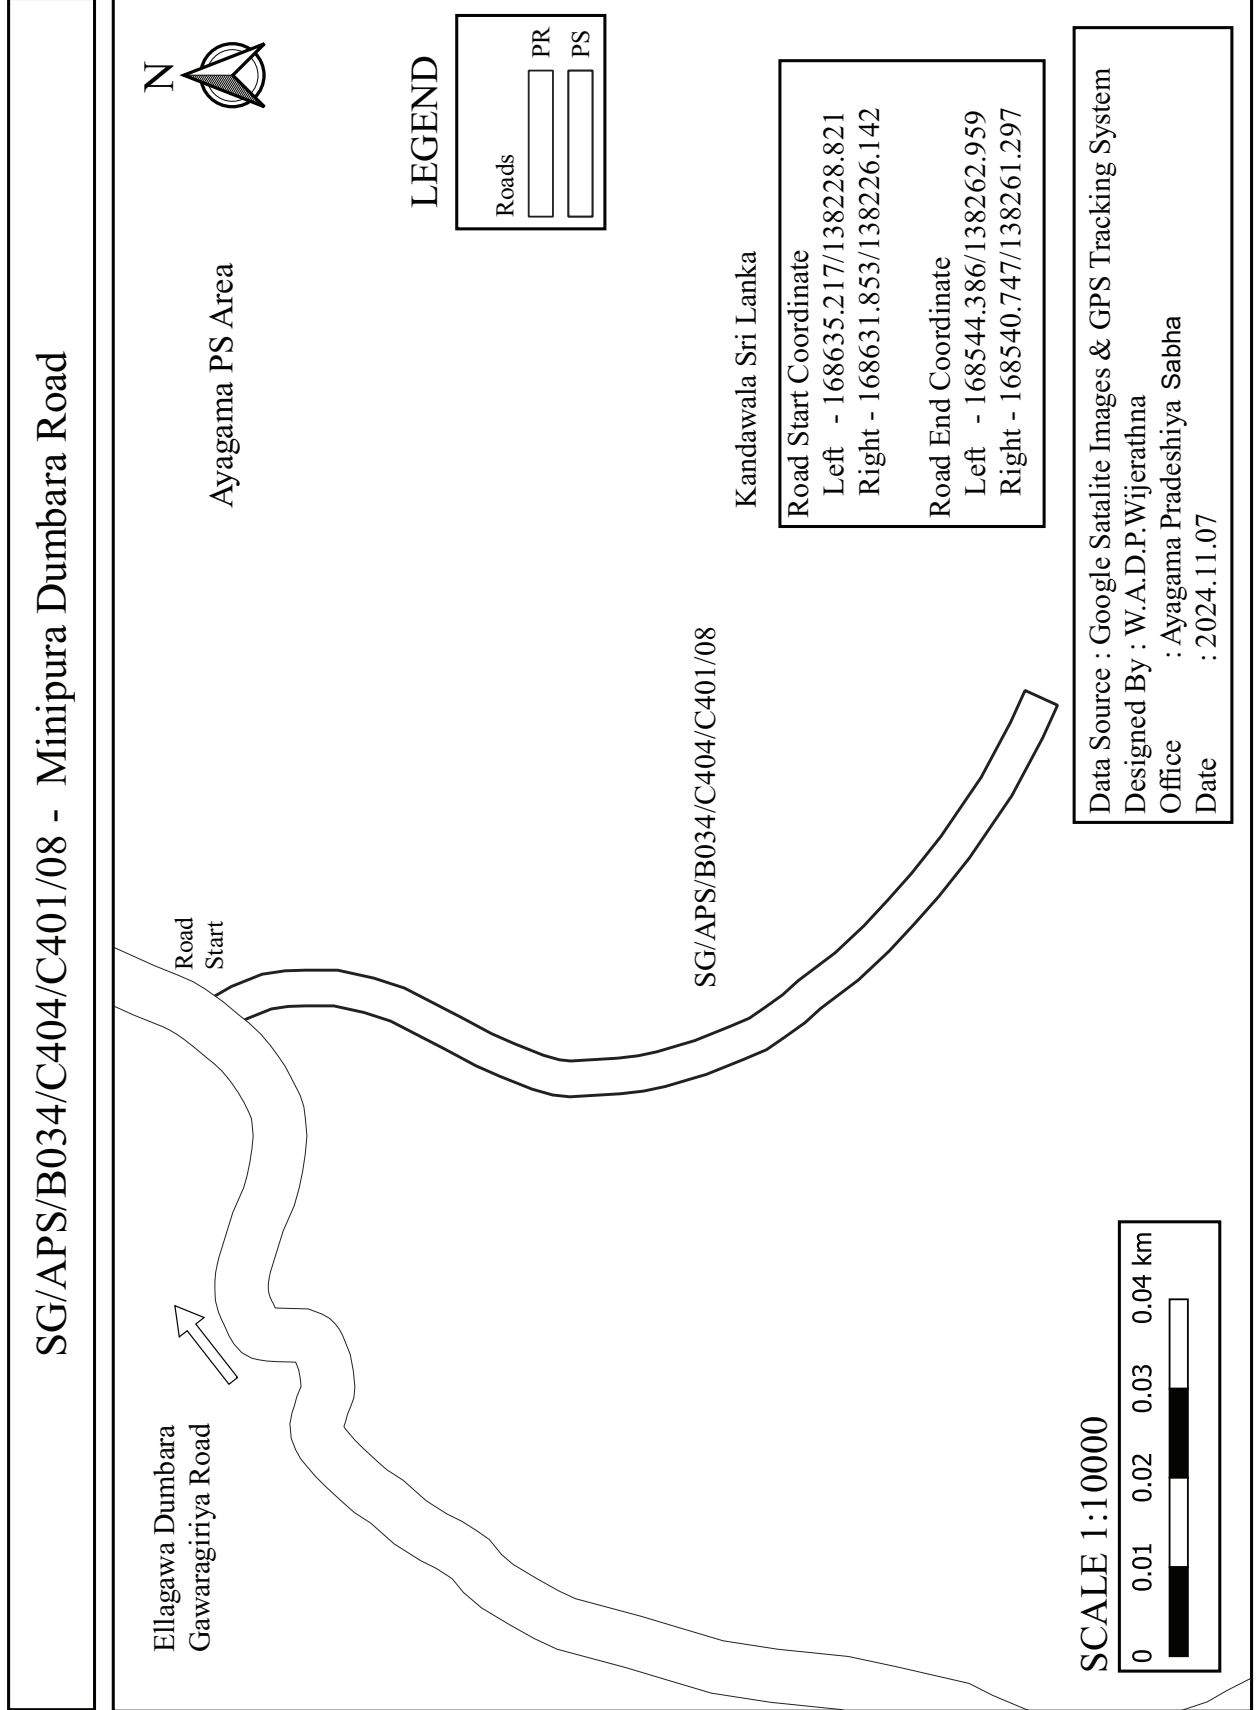



SG/APS/B034/C404/C401/09 - Minipura Dumbara Ataheraliyagoda Road

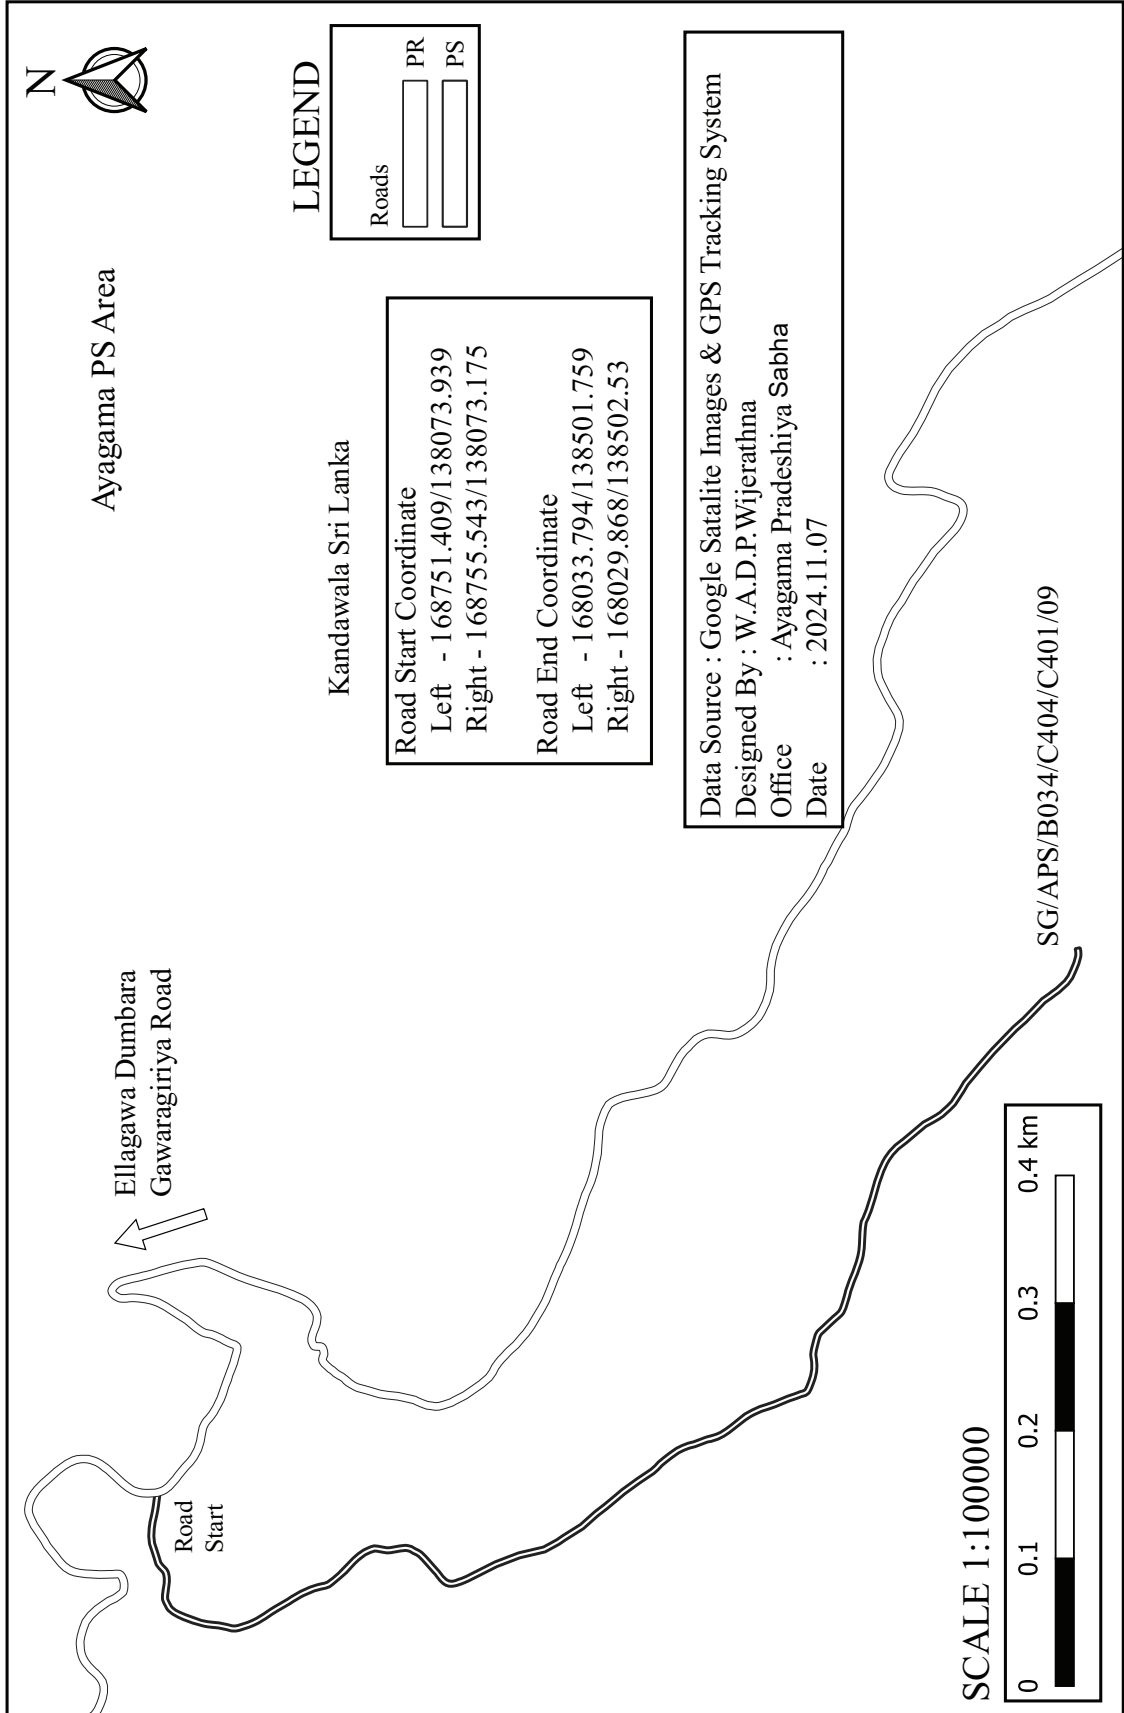


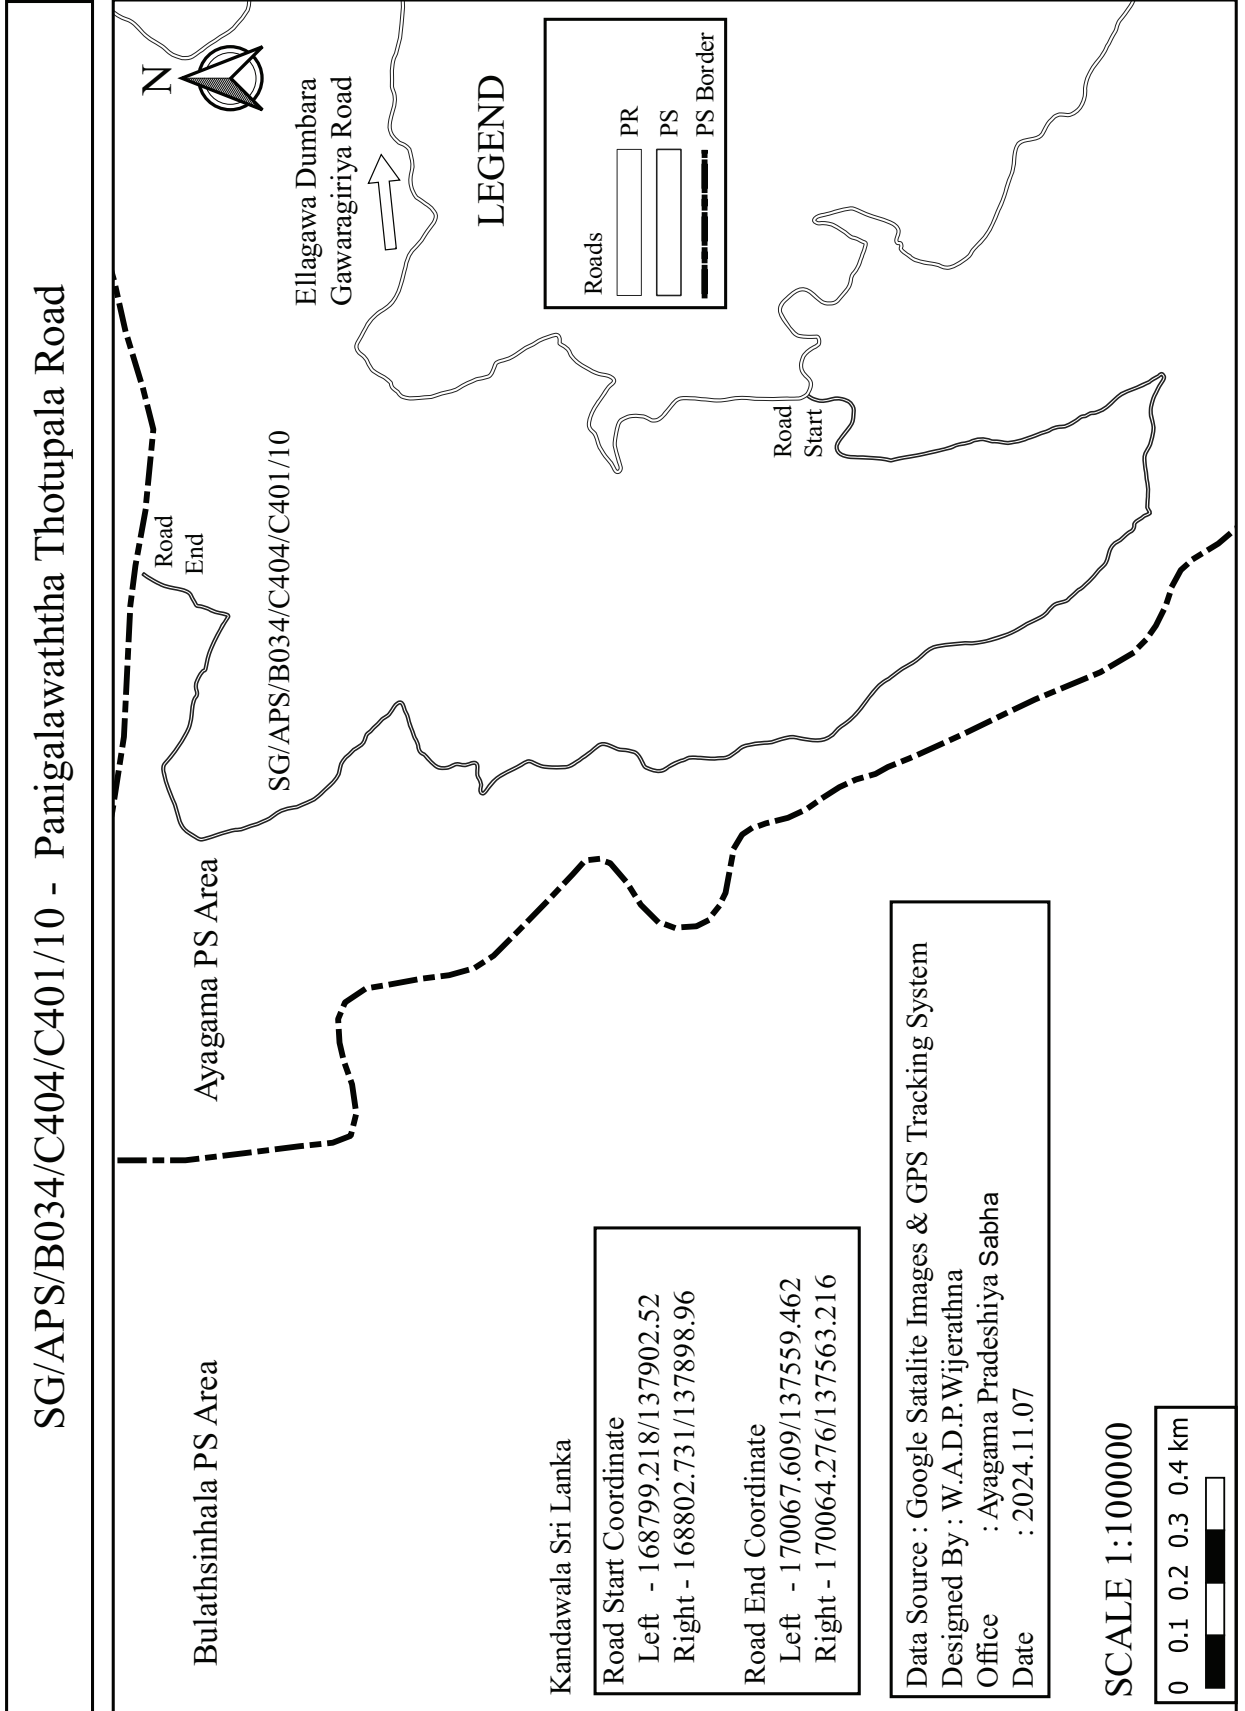


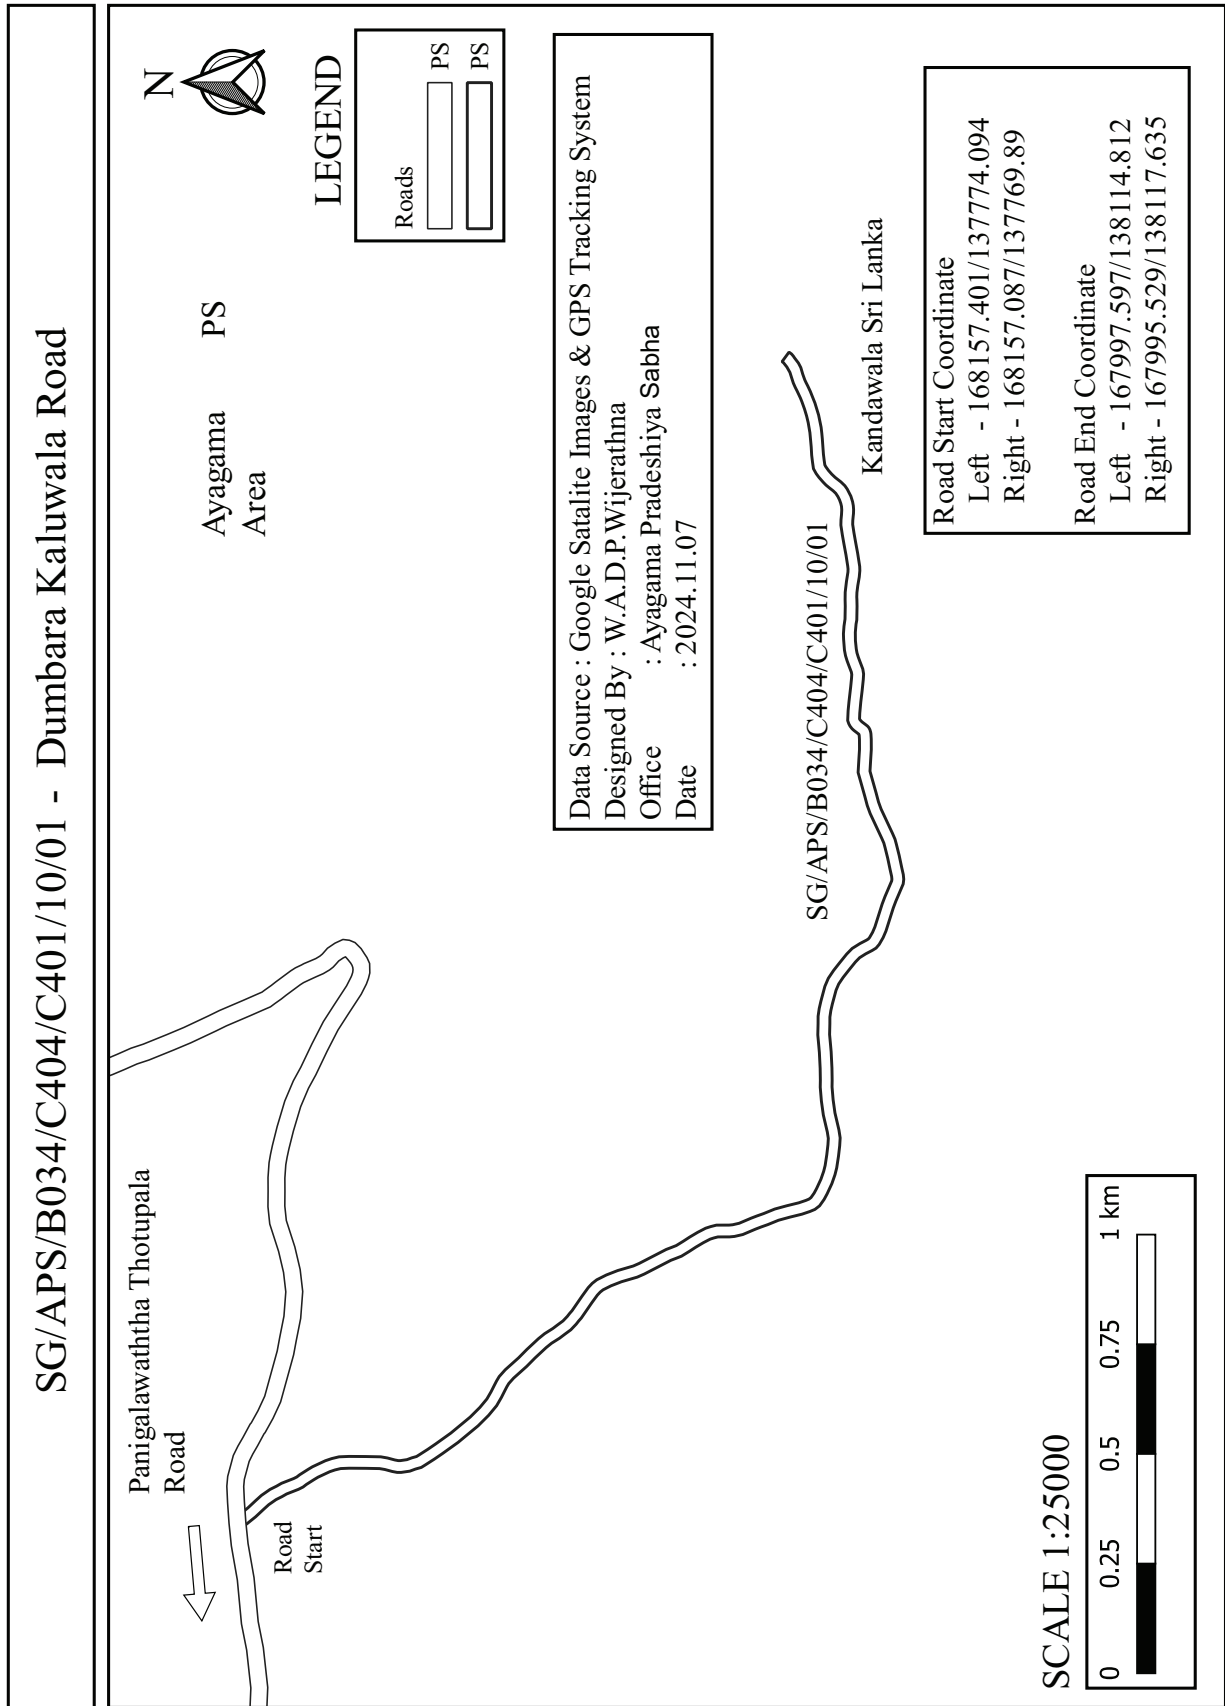


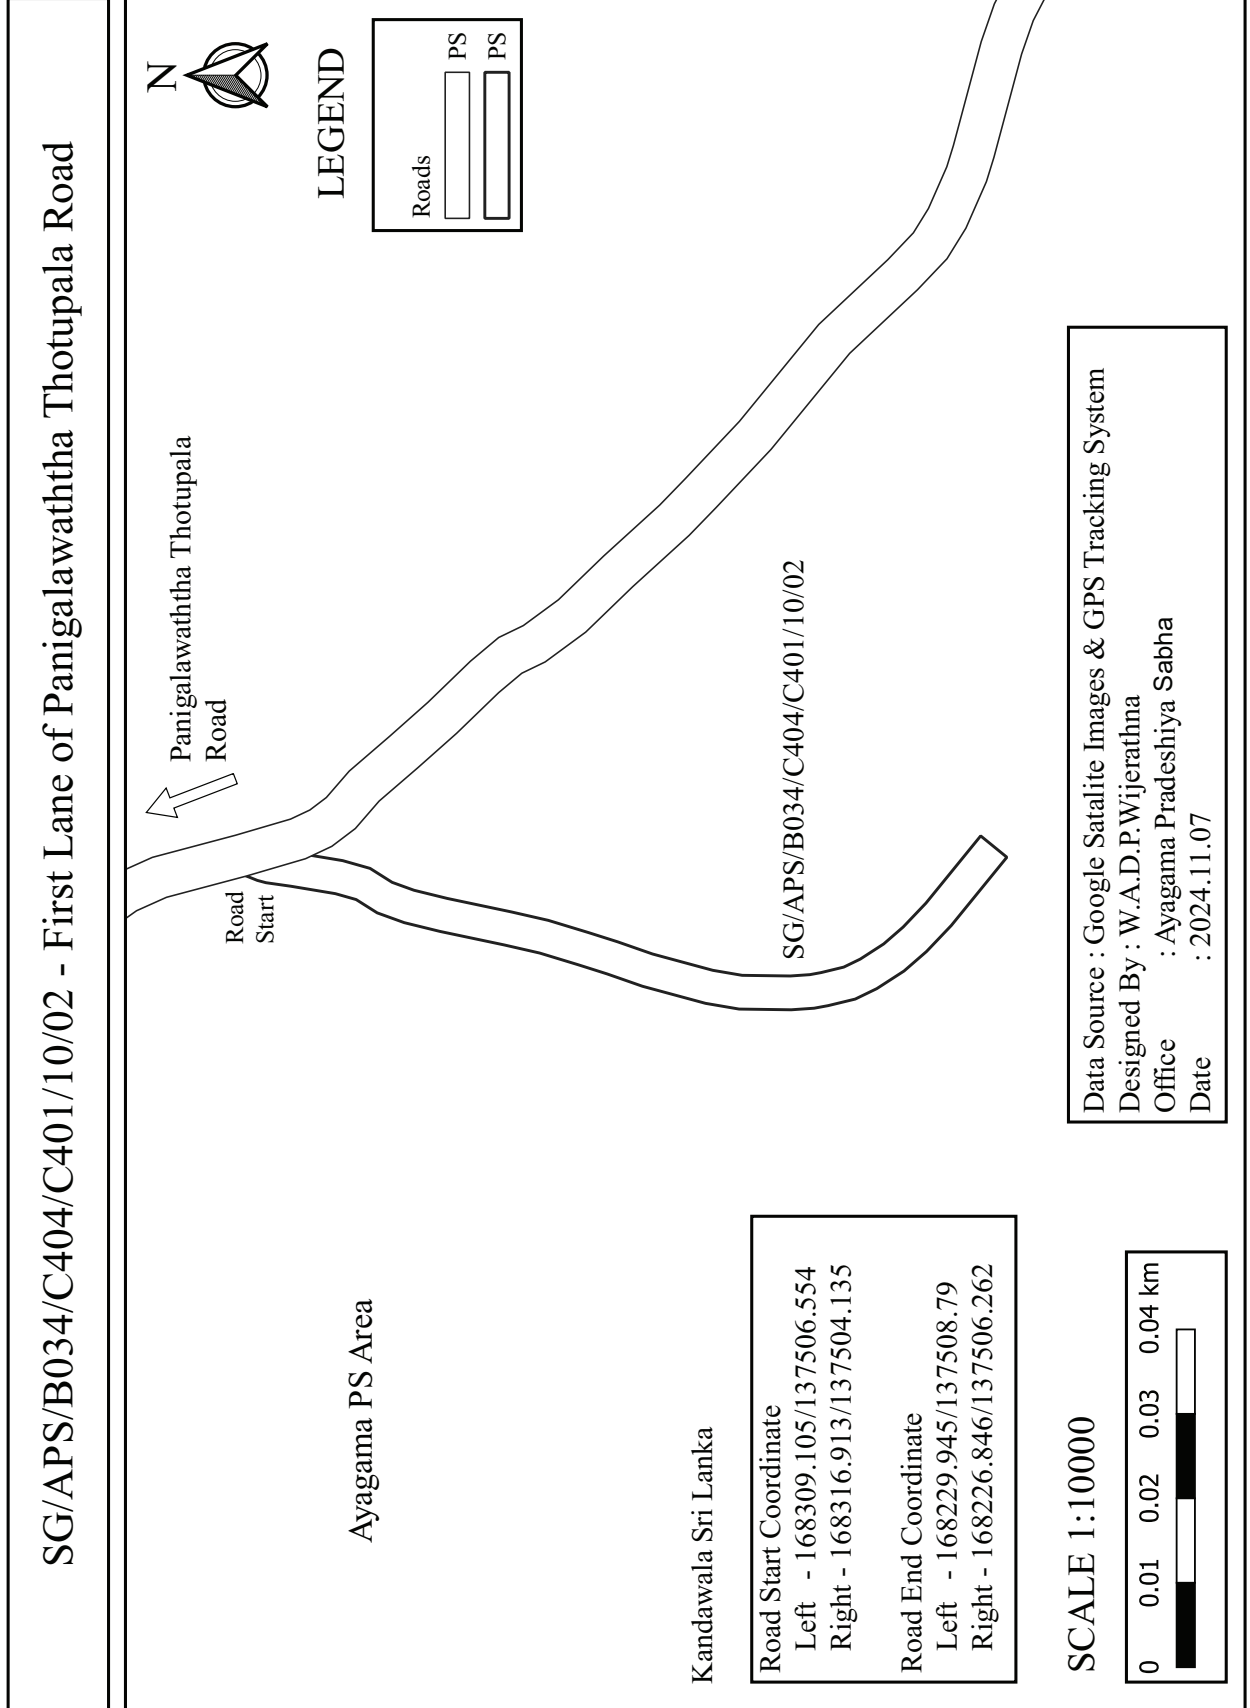


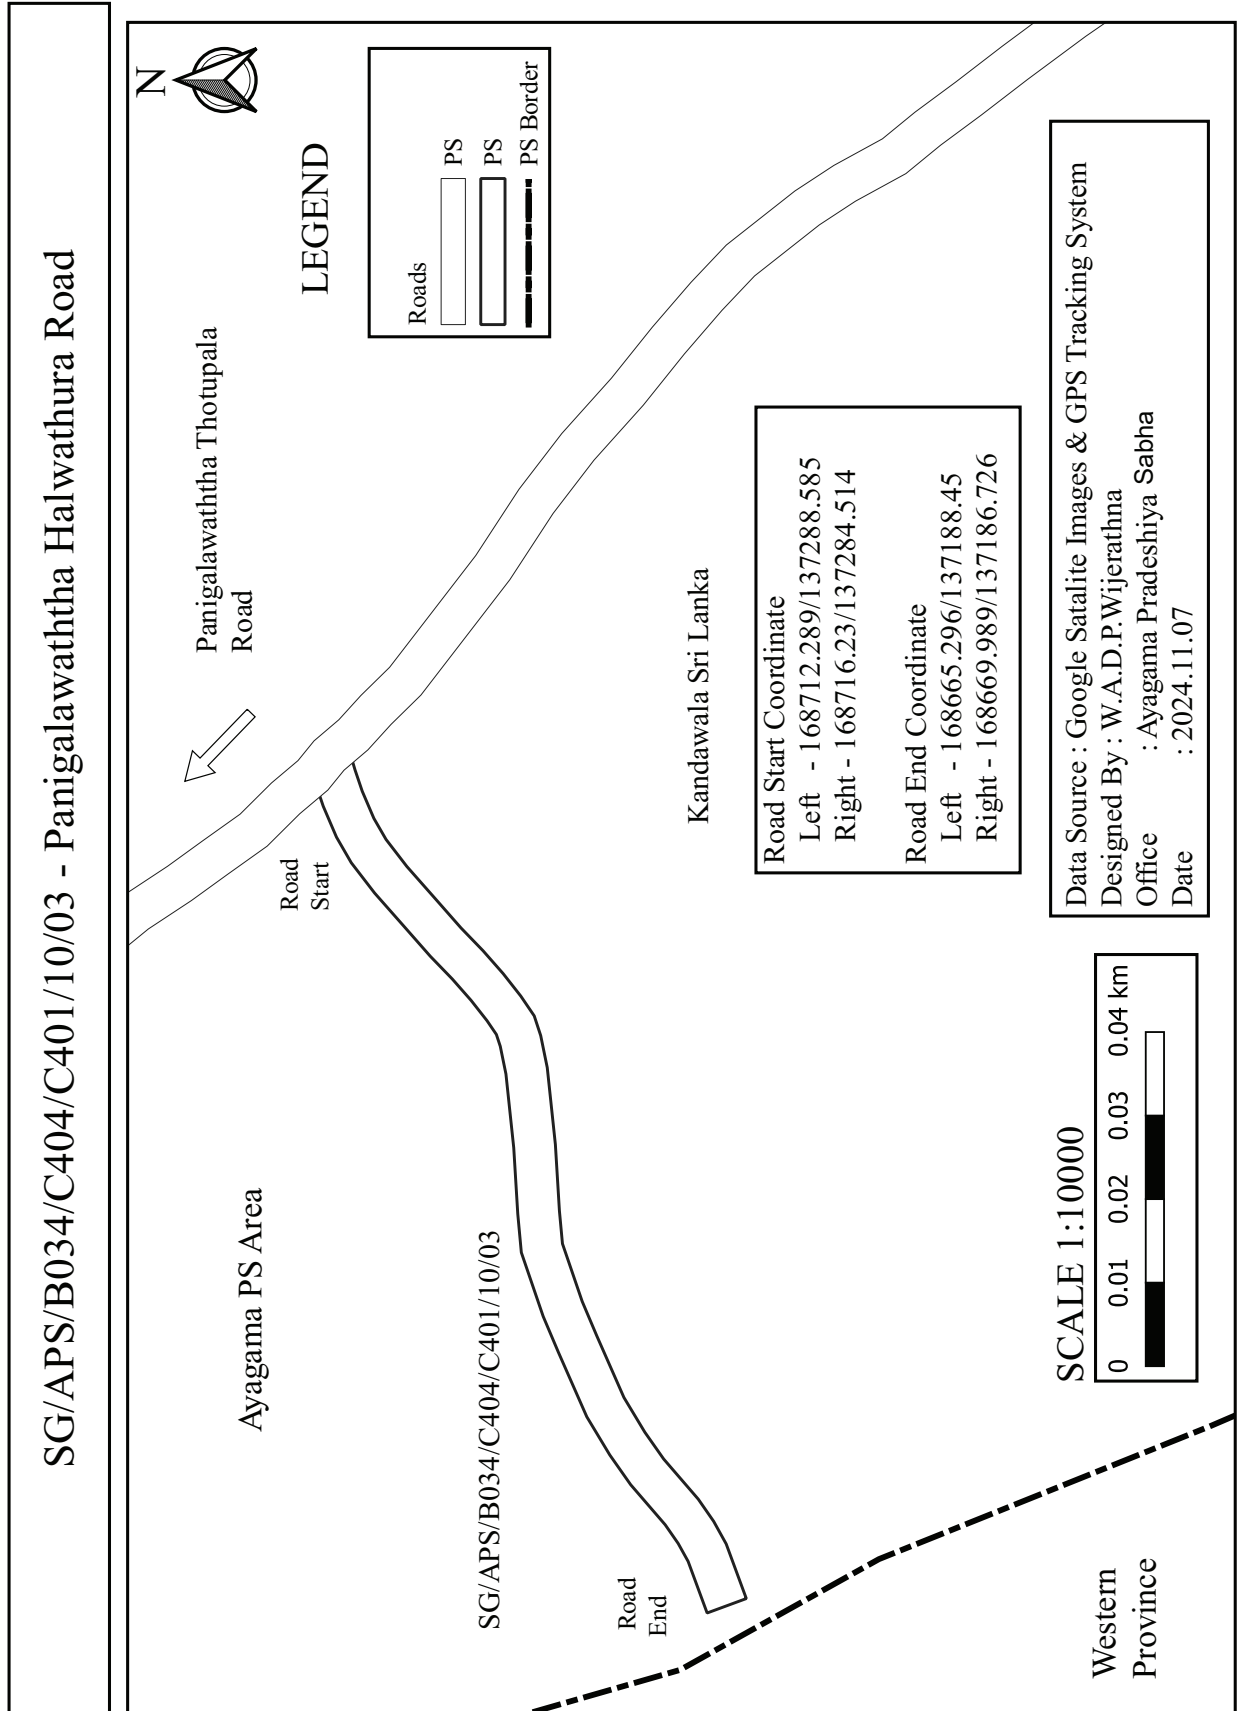


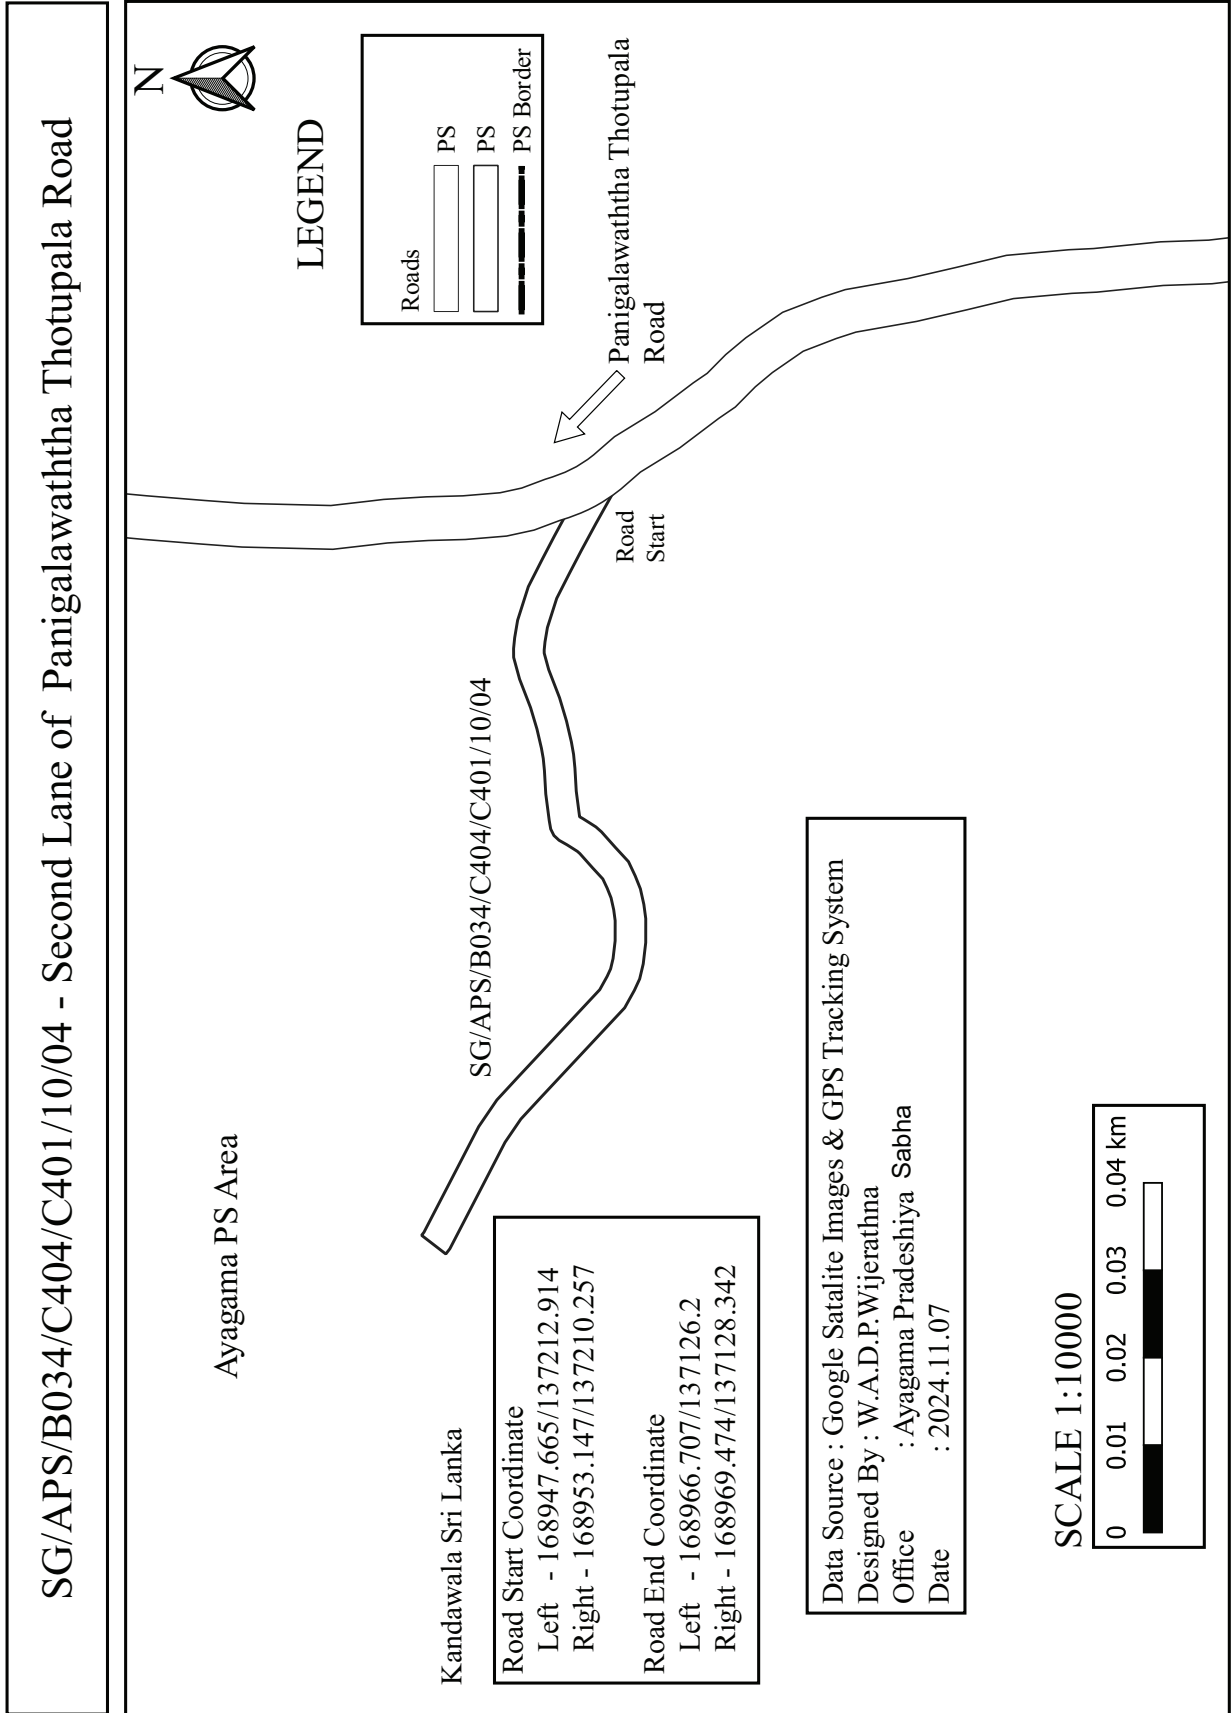


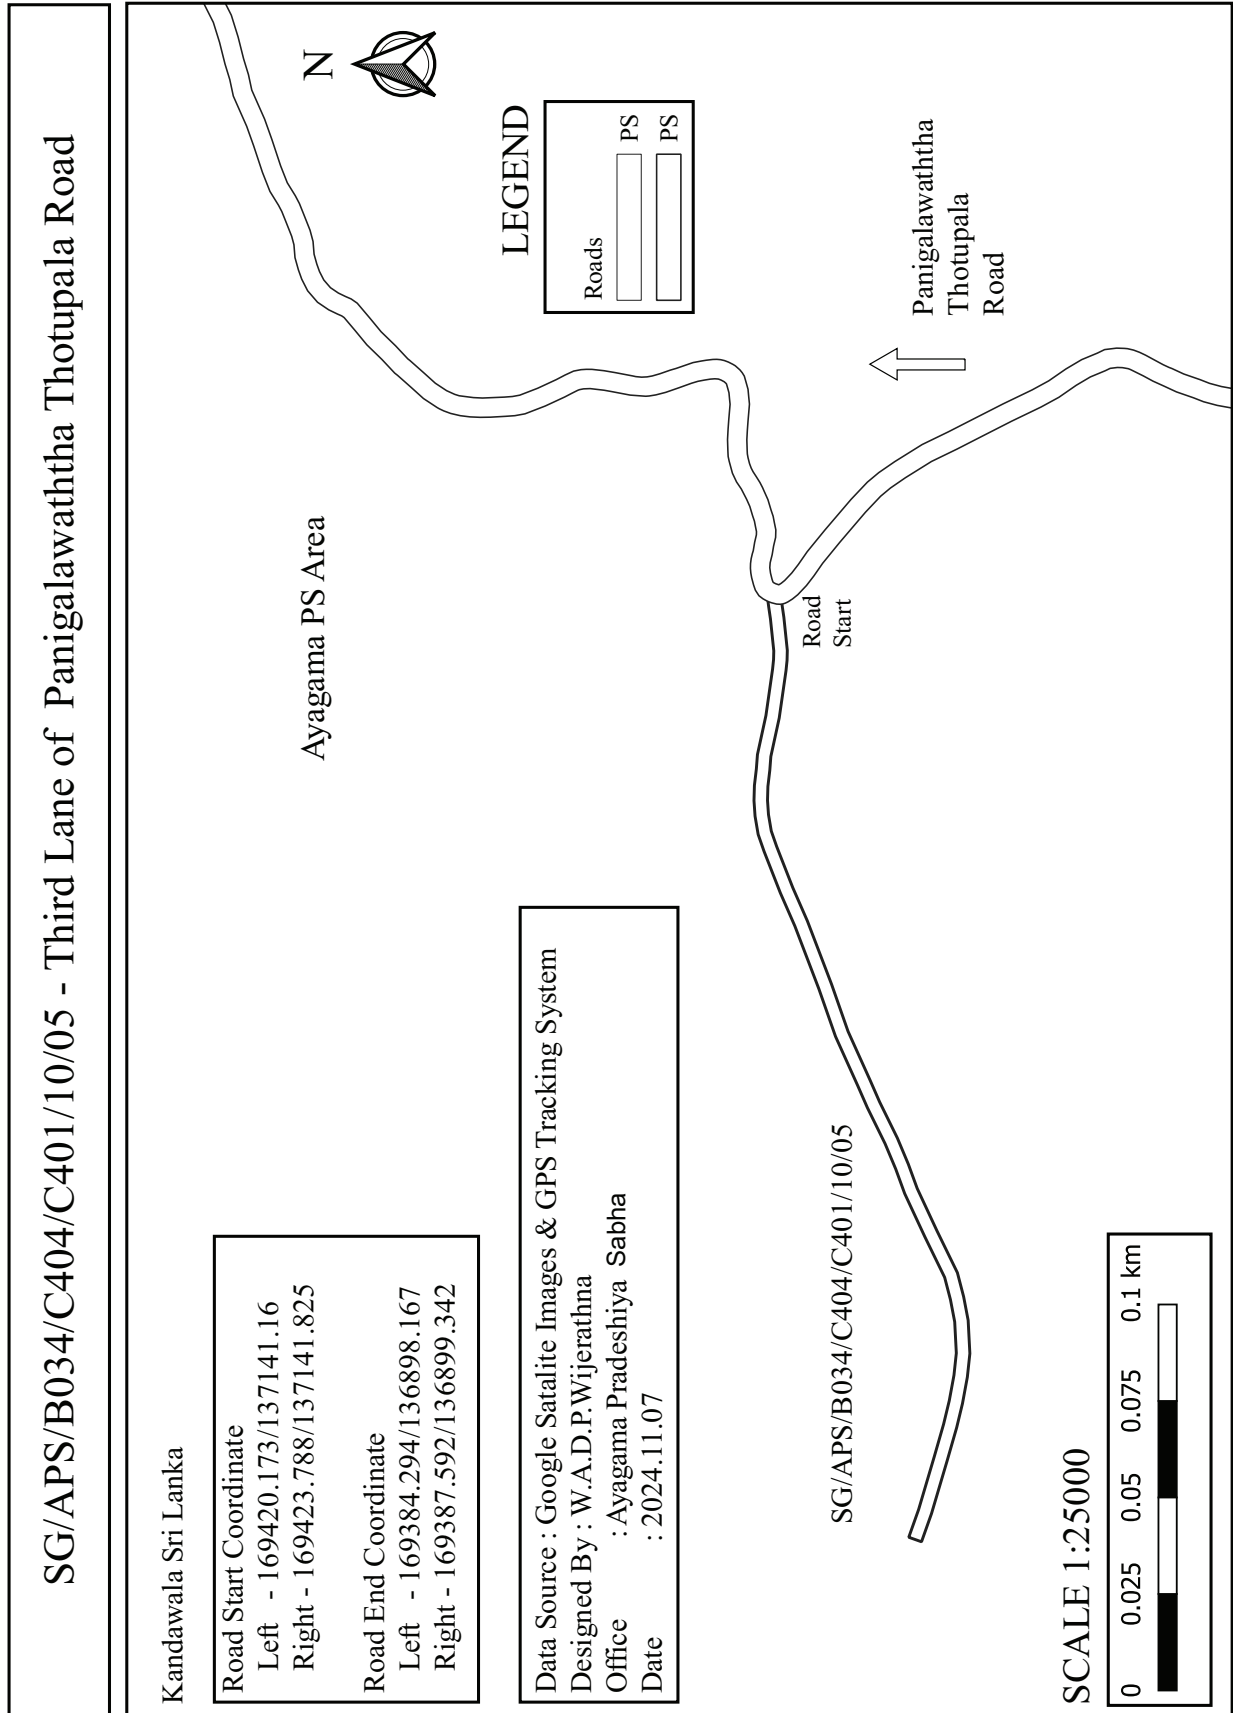


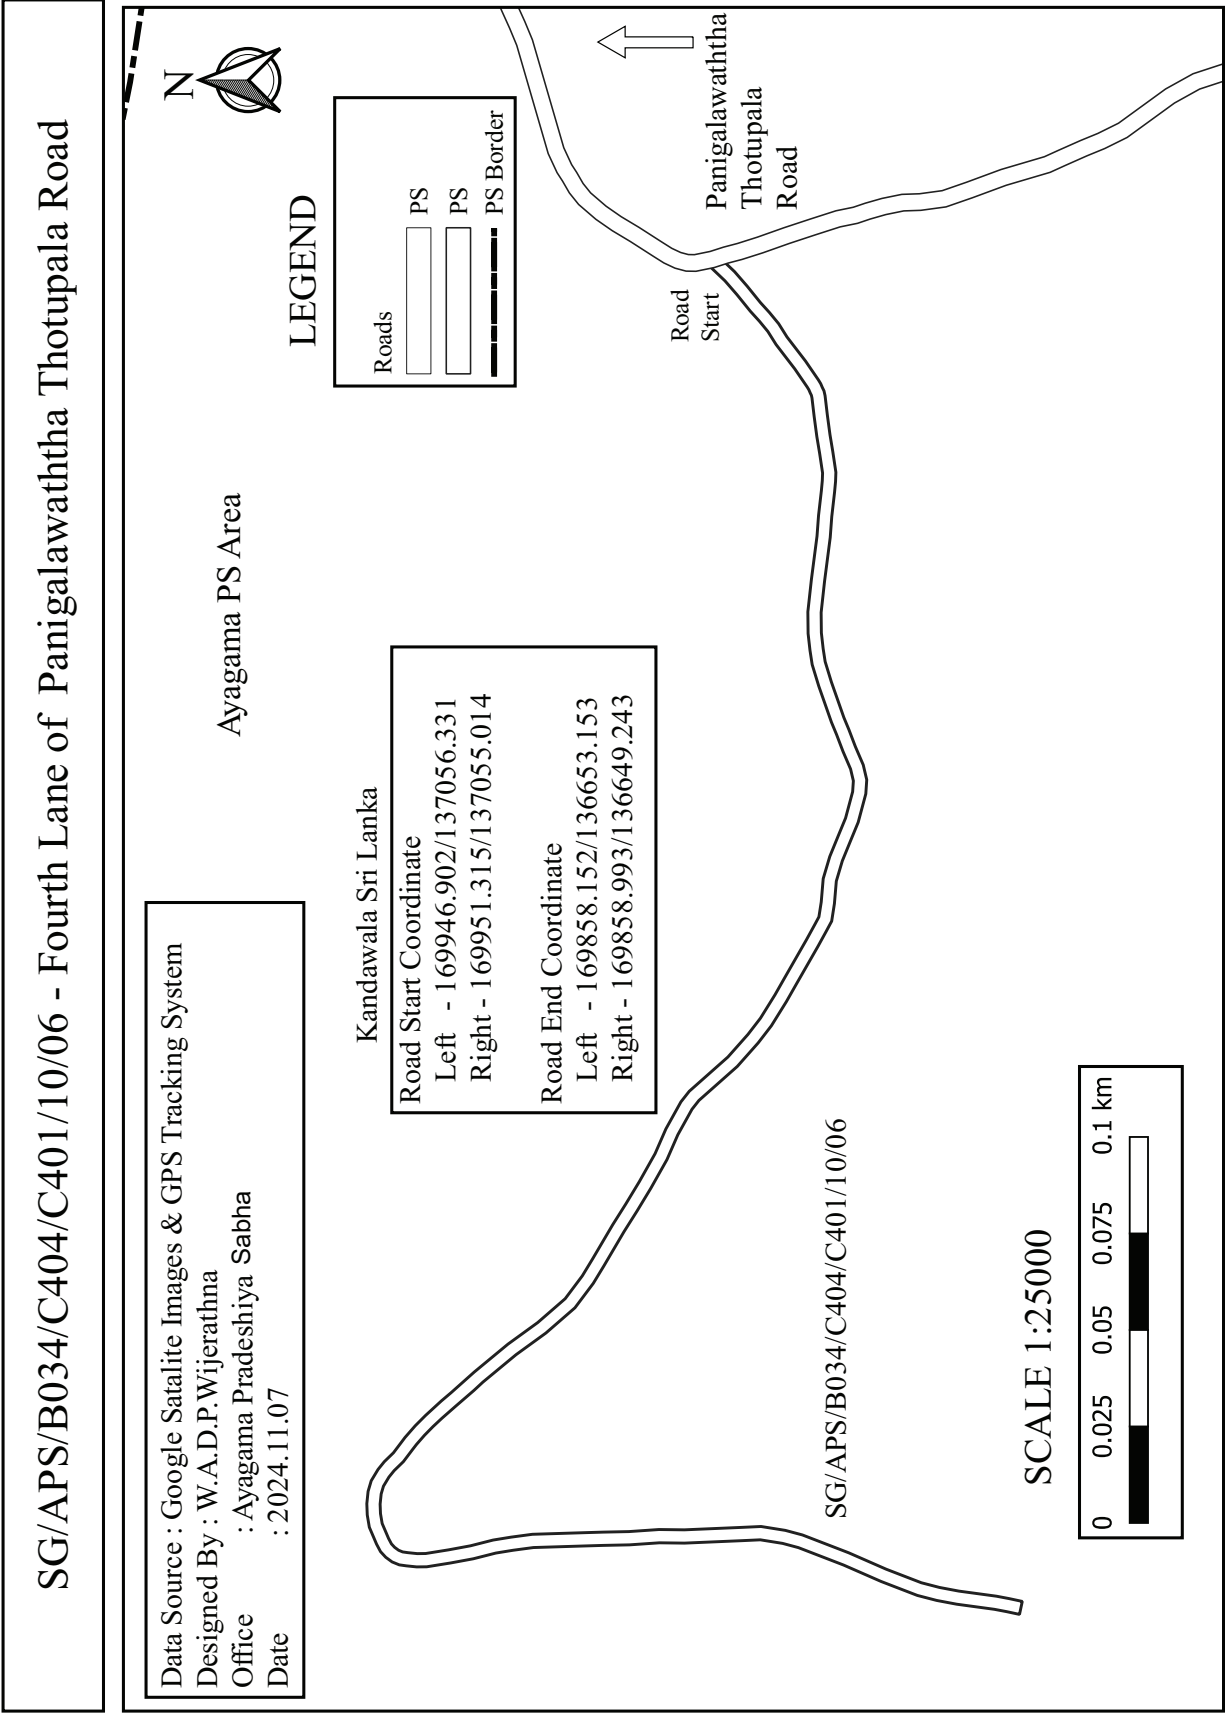


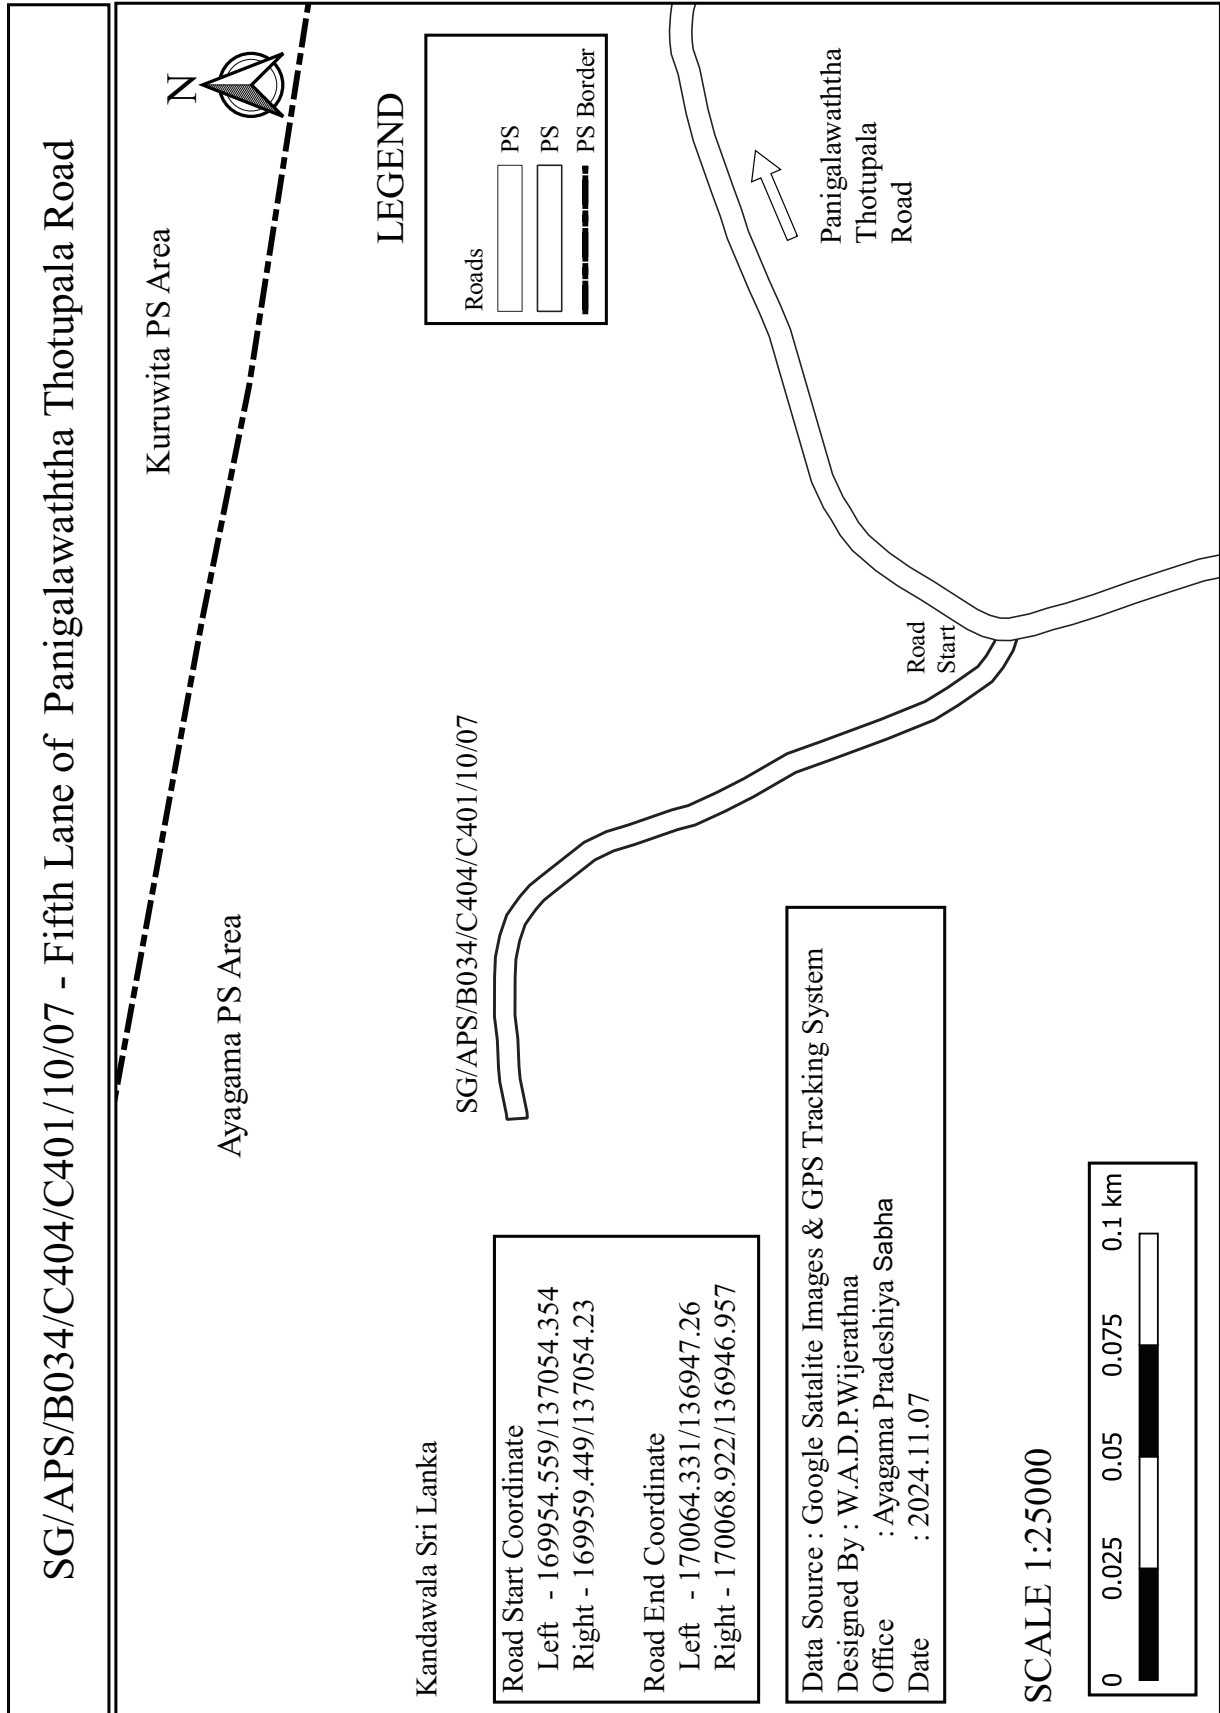


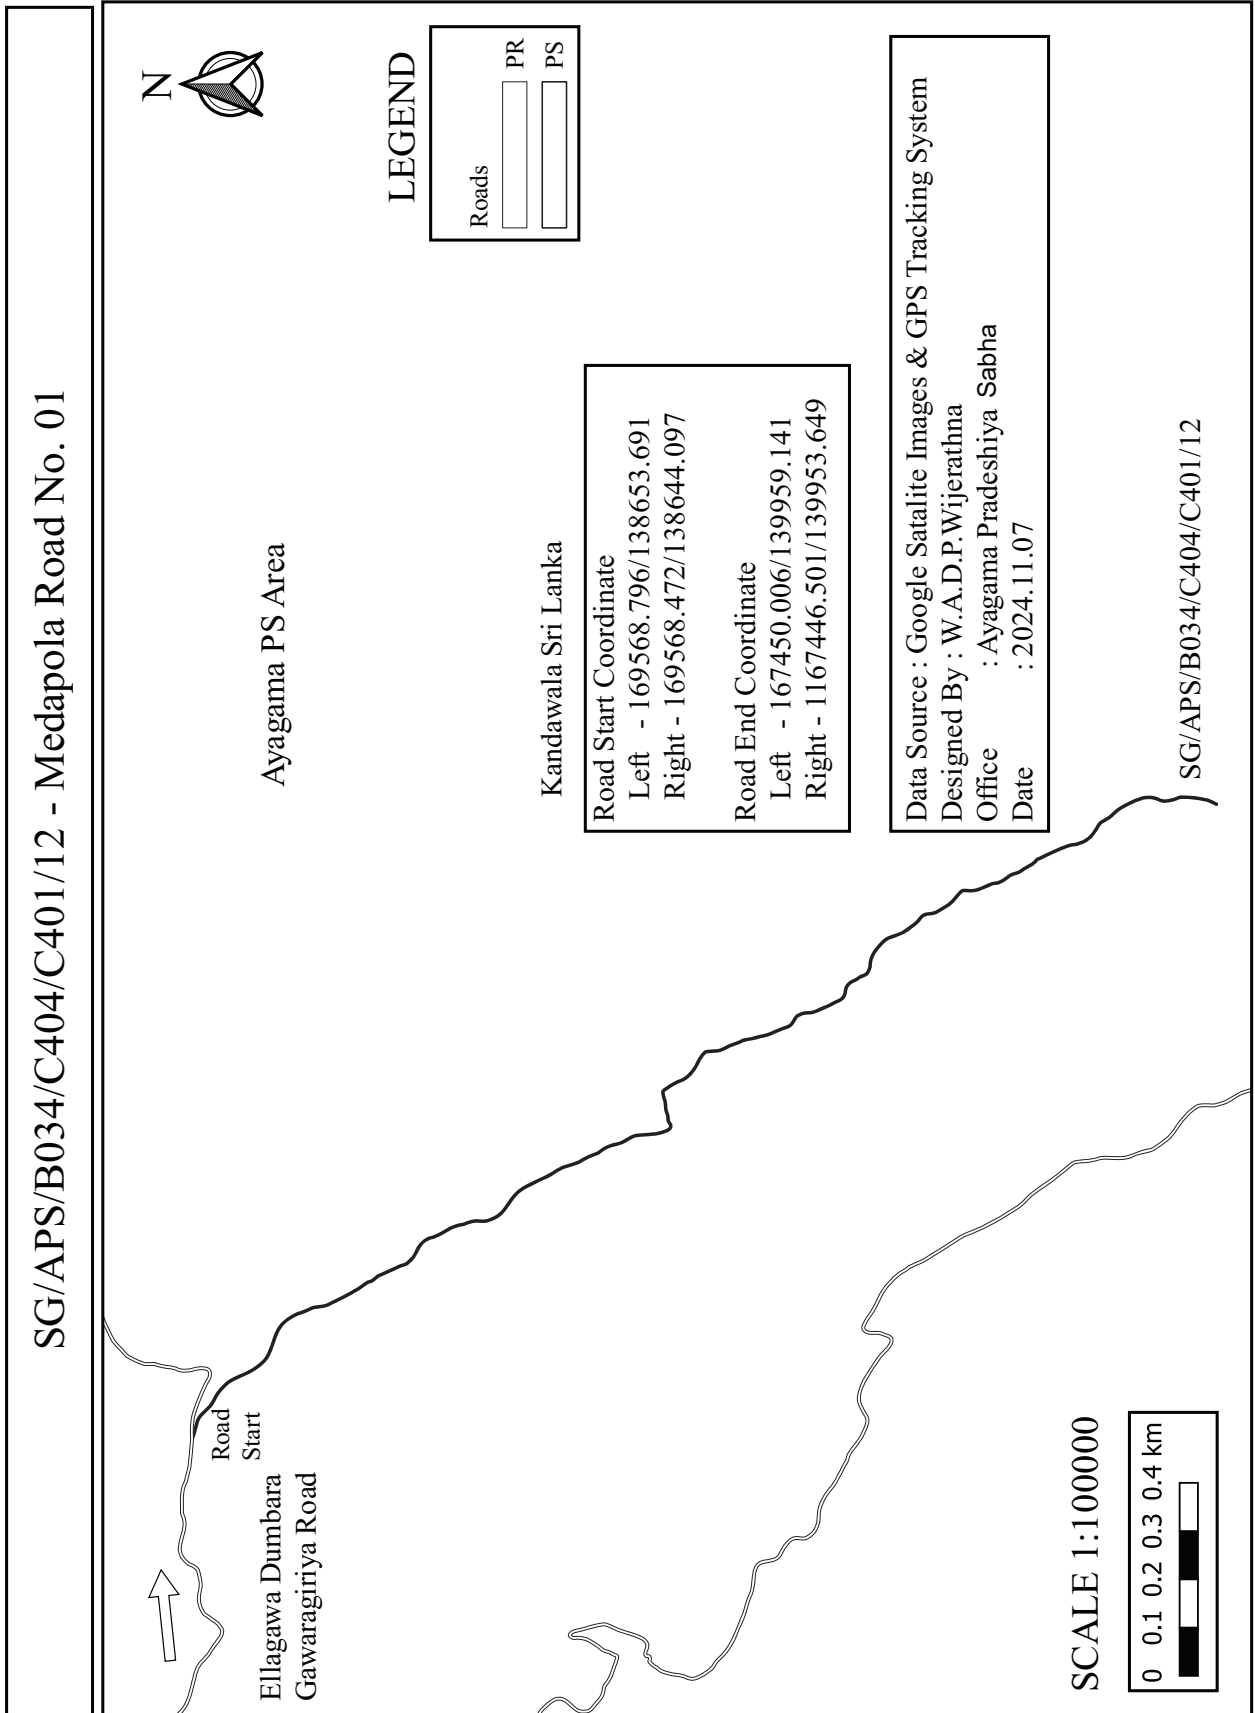


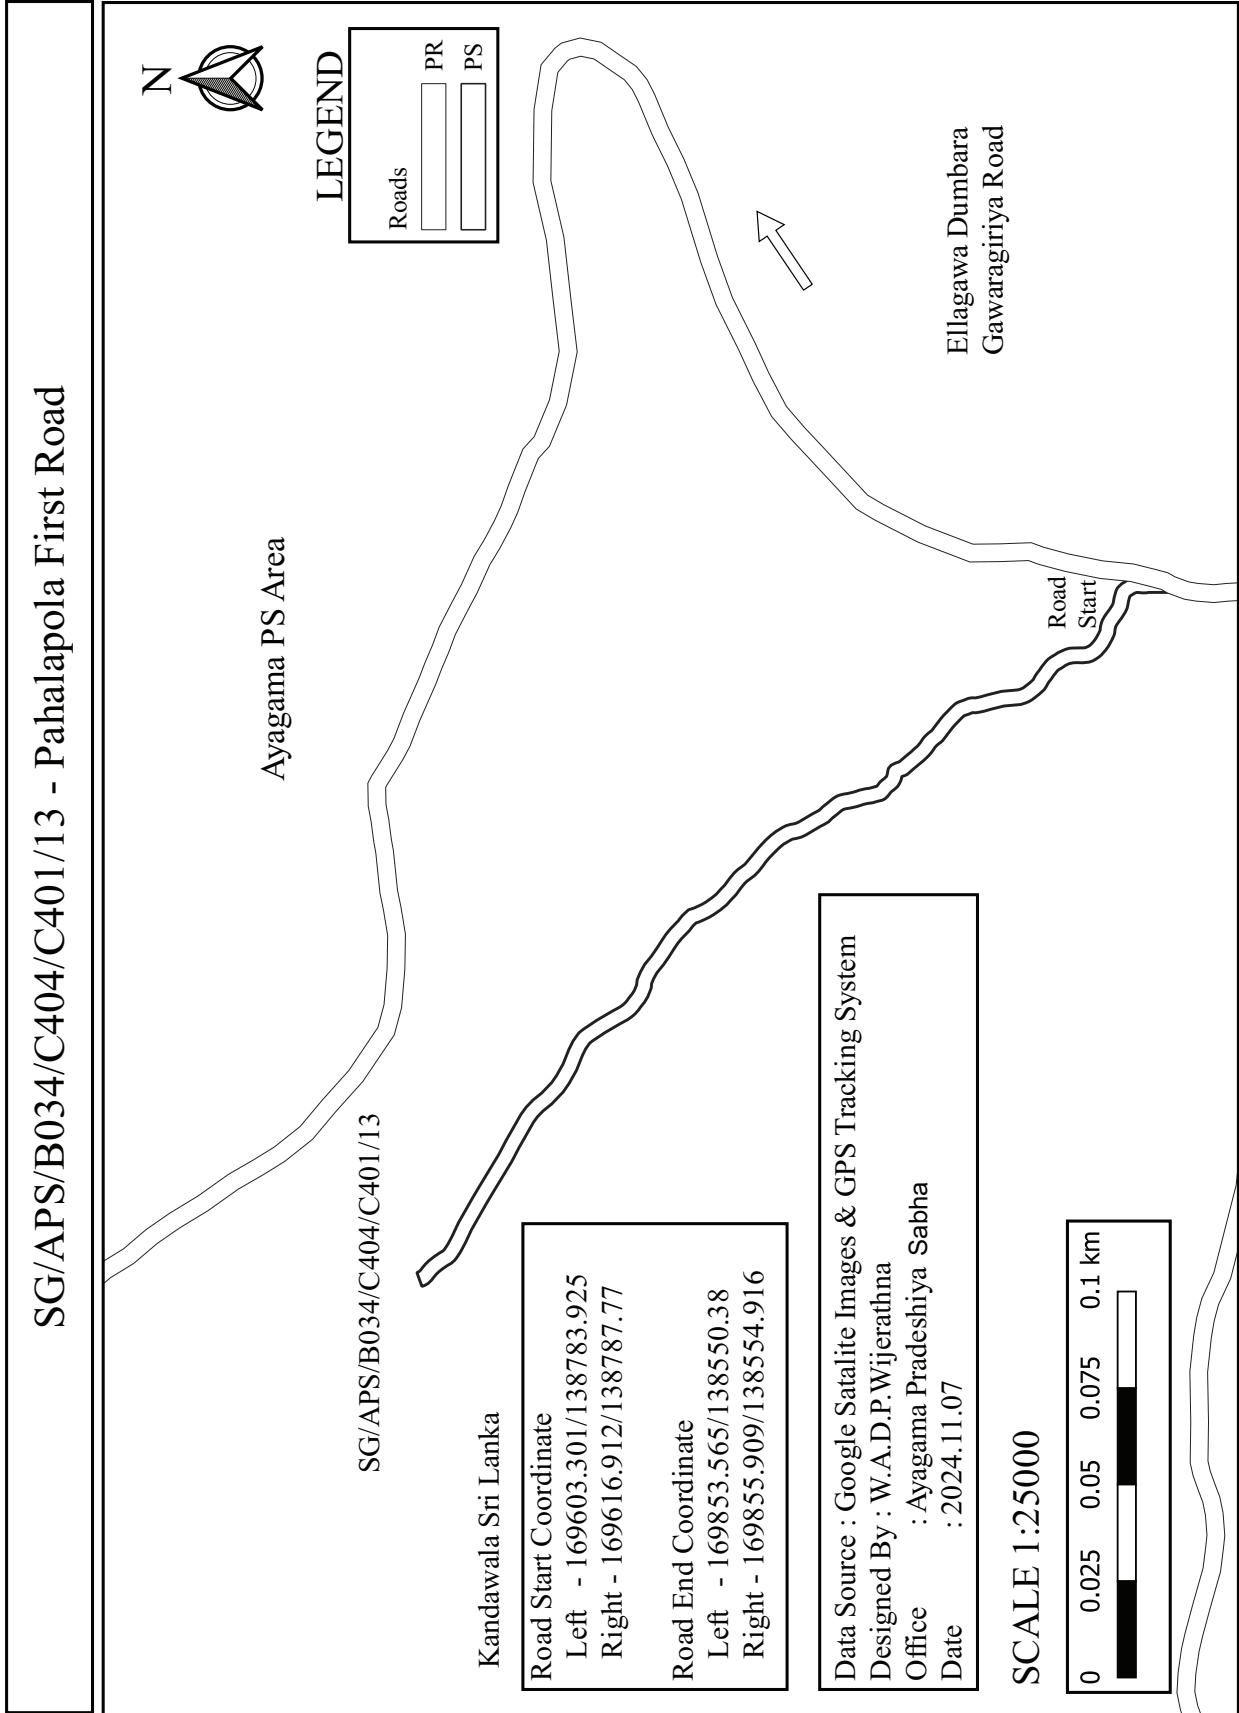


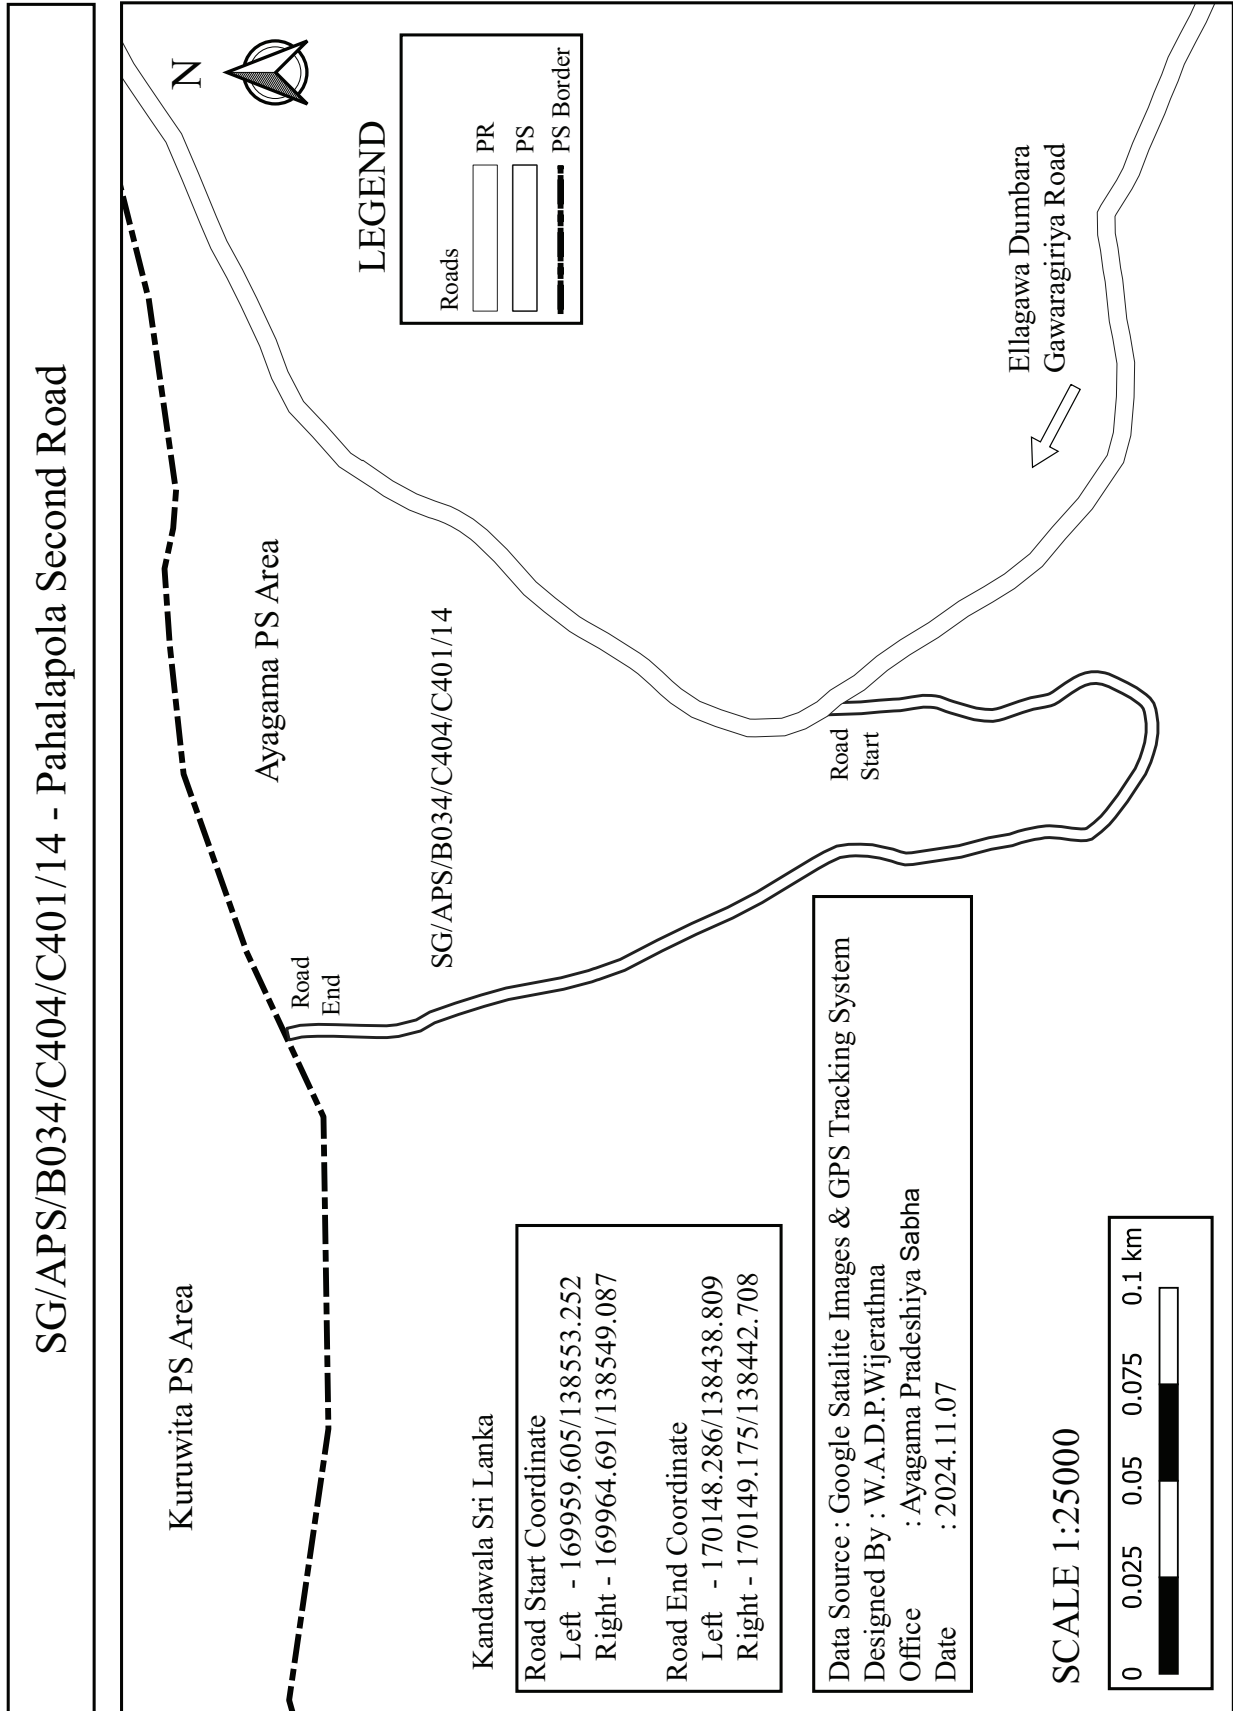


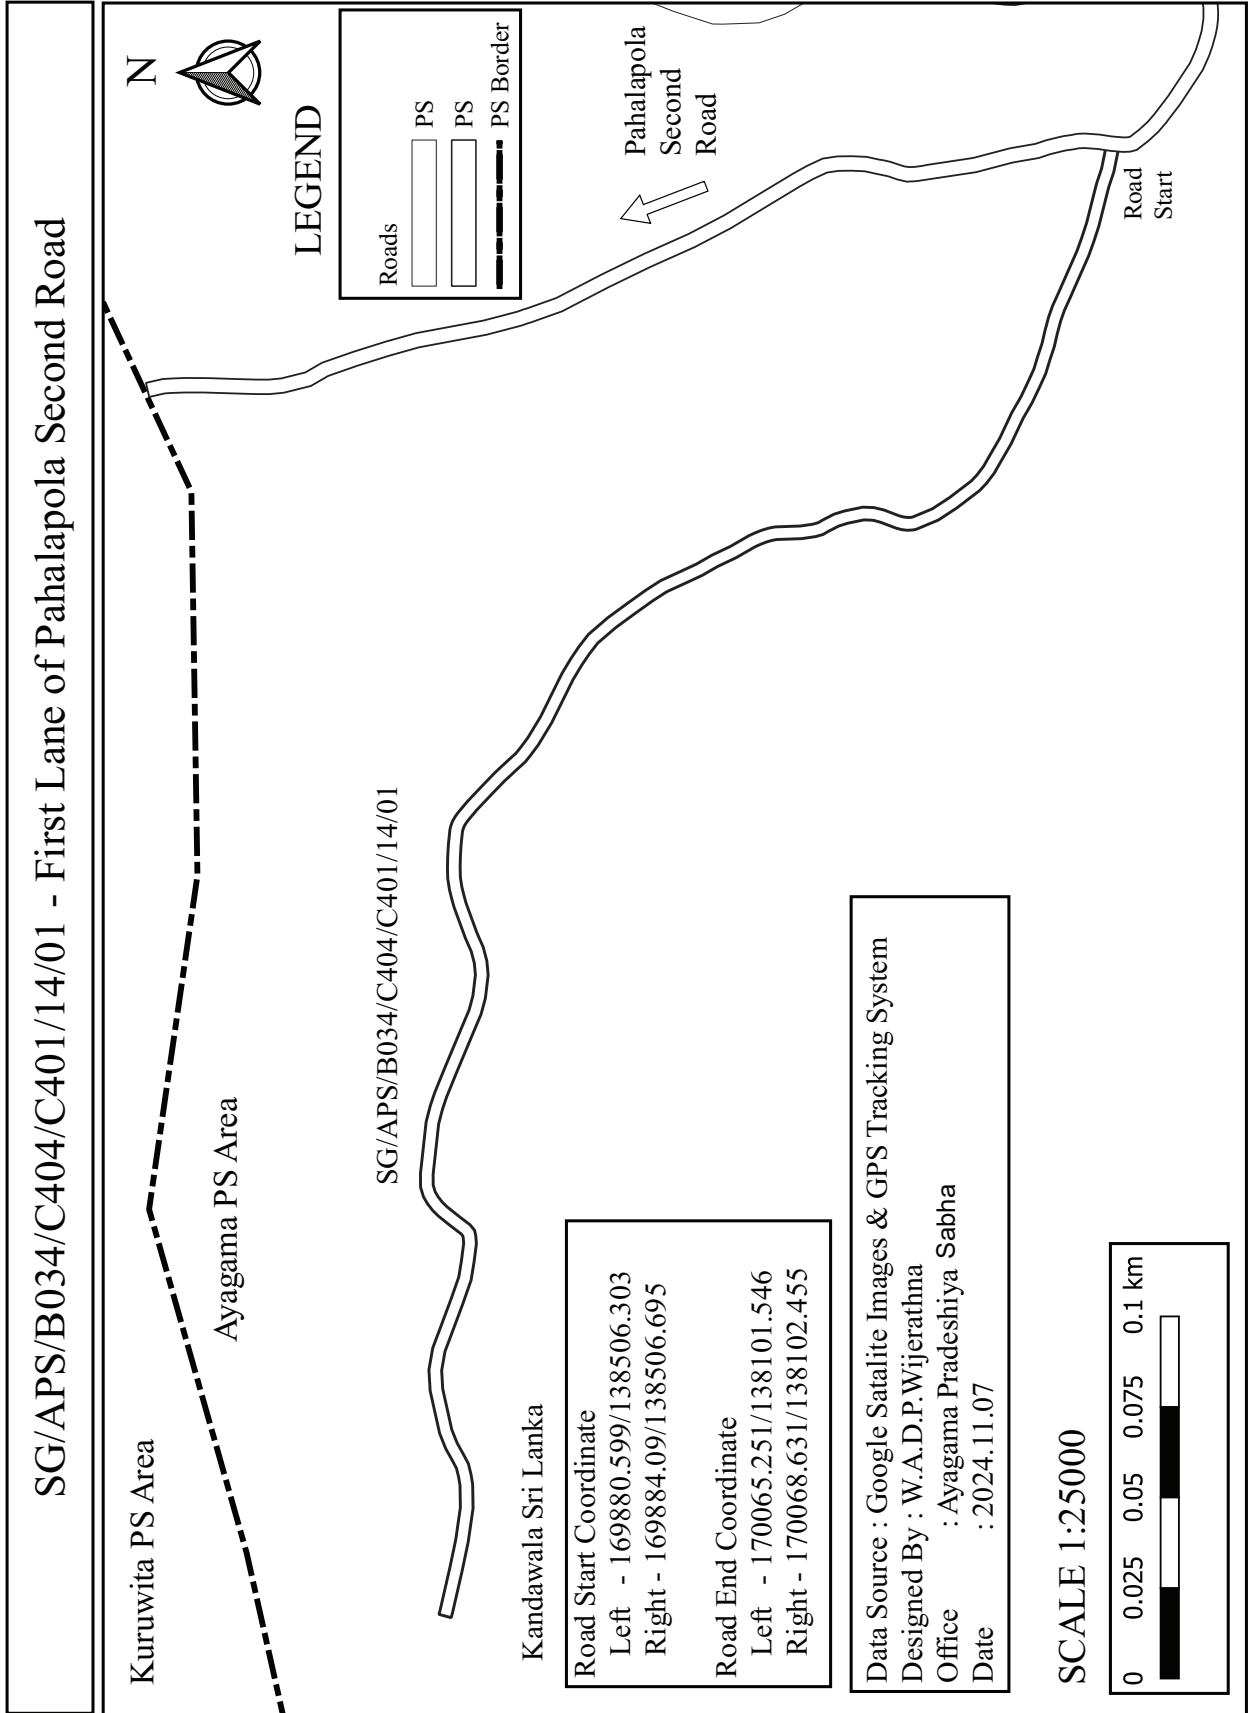


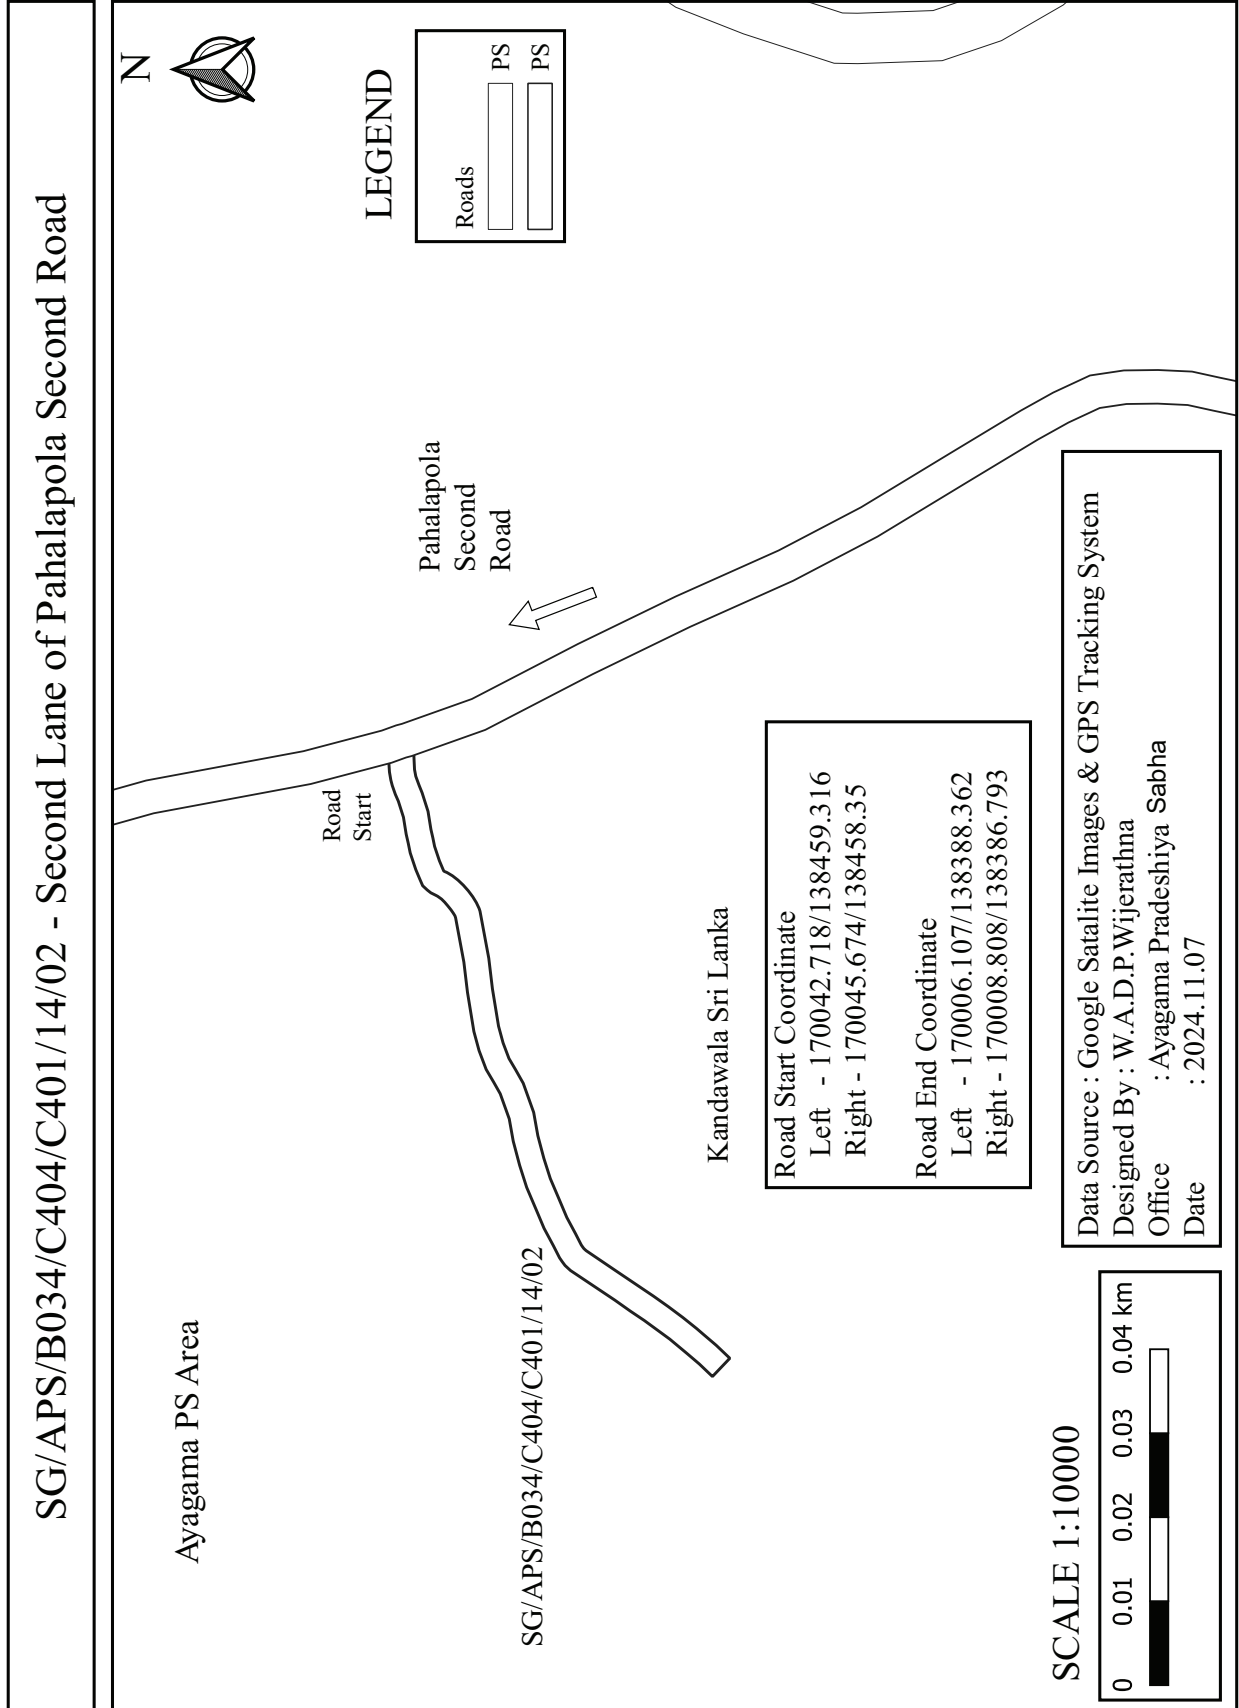


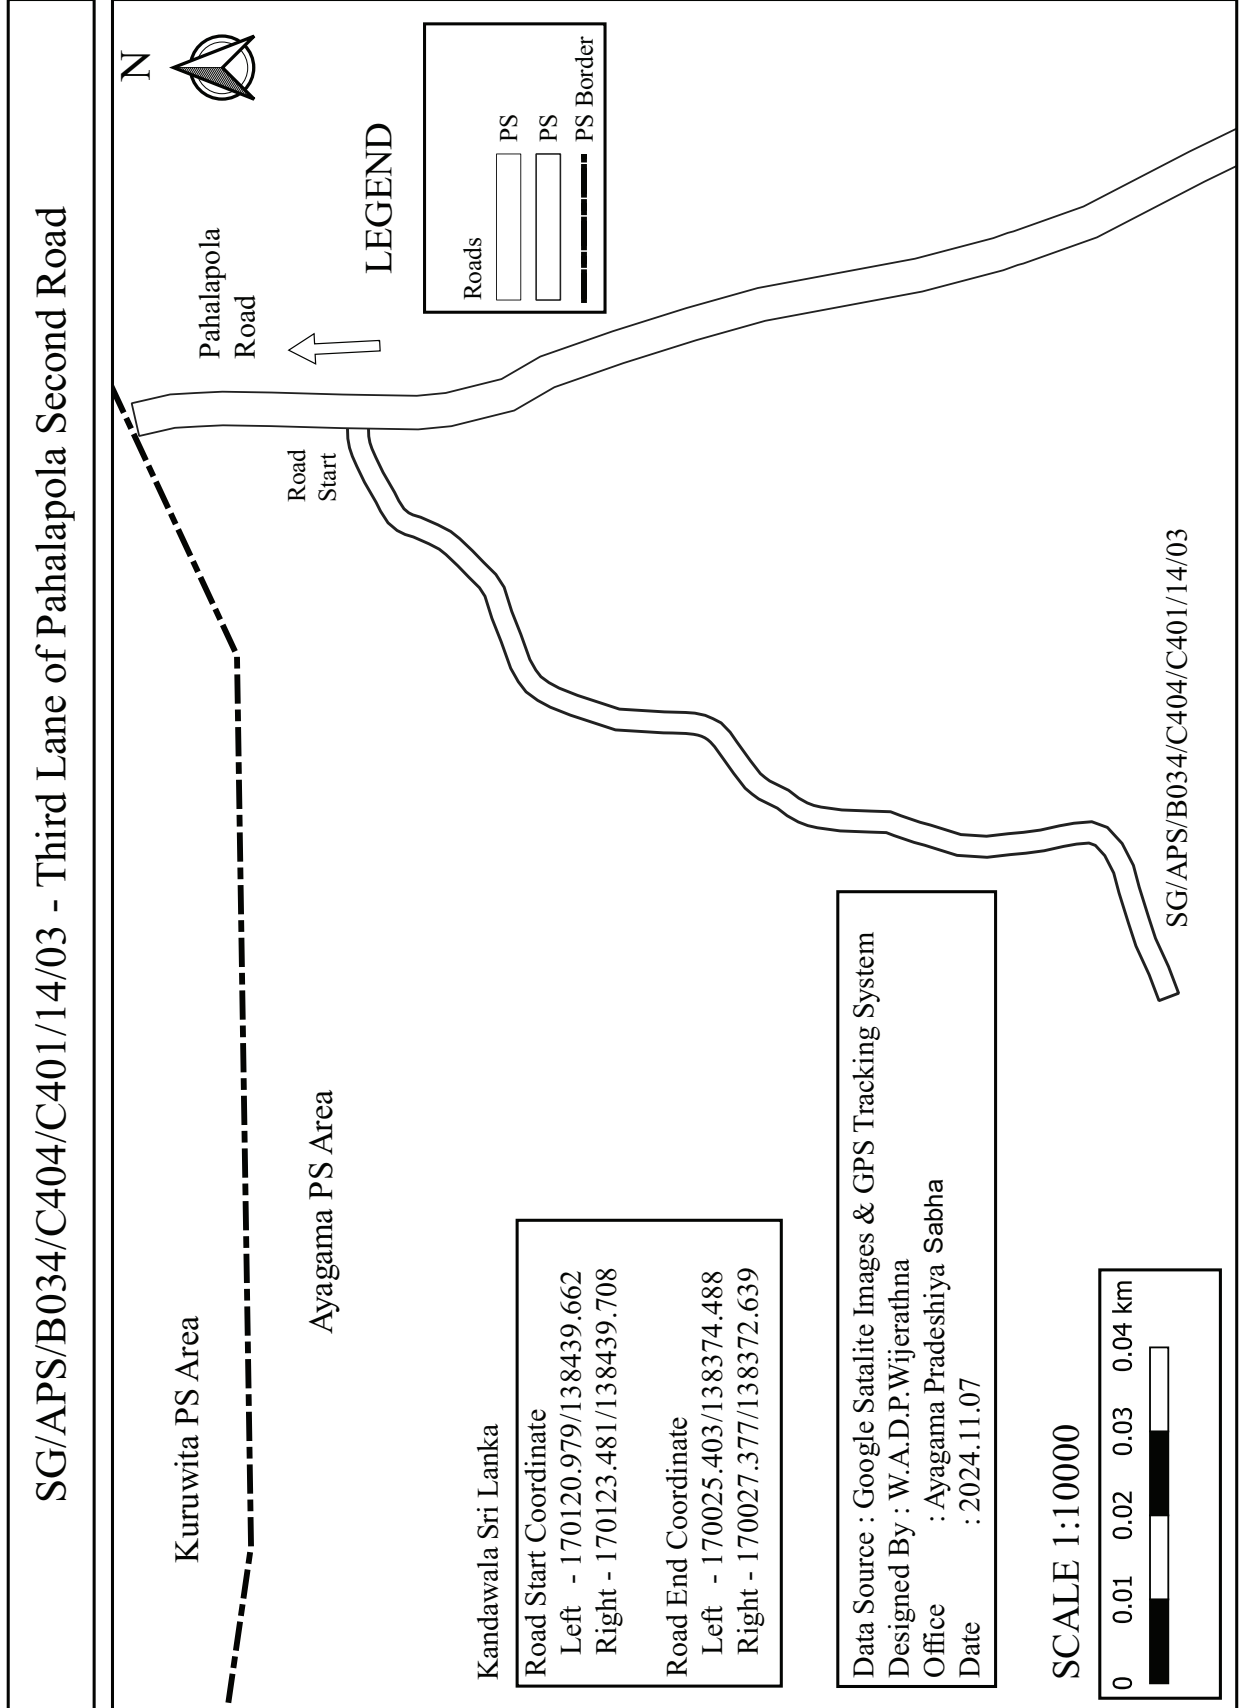


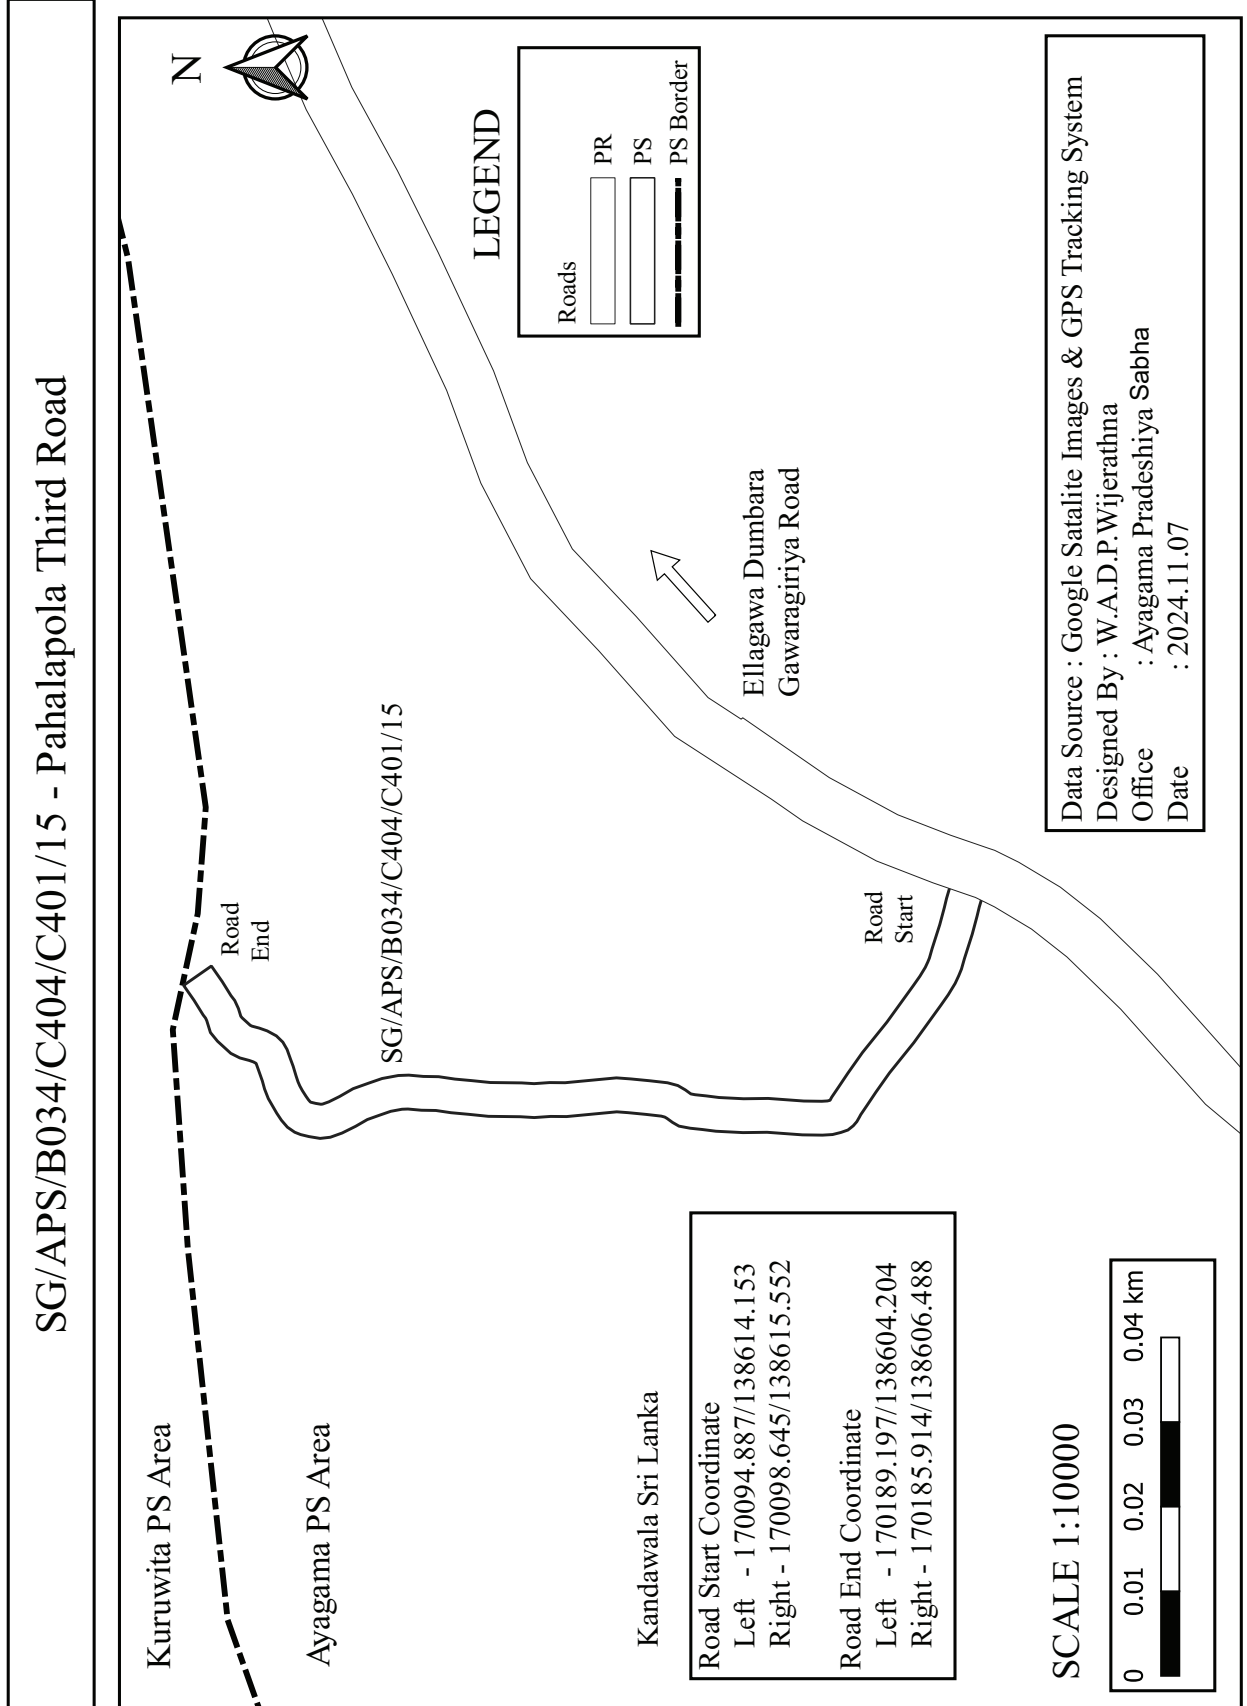


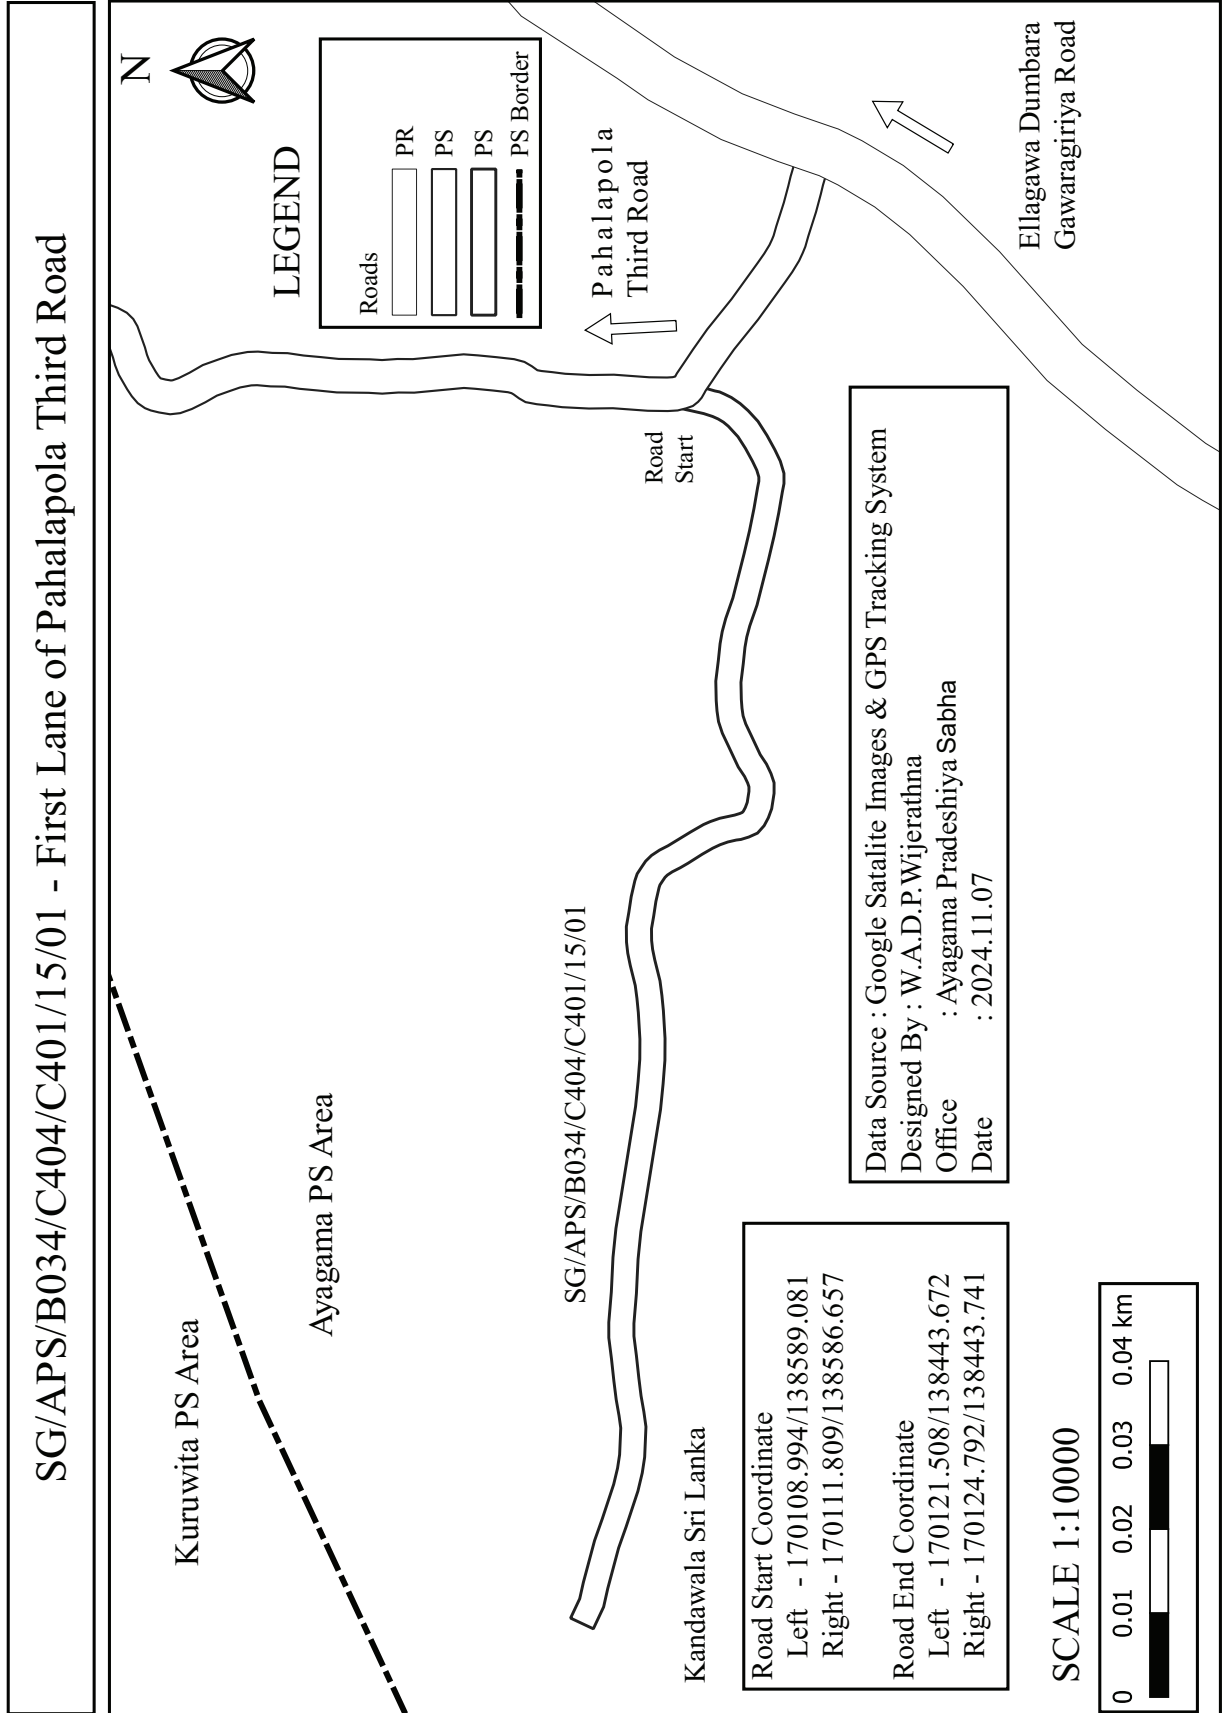


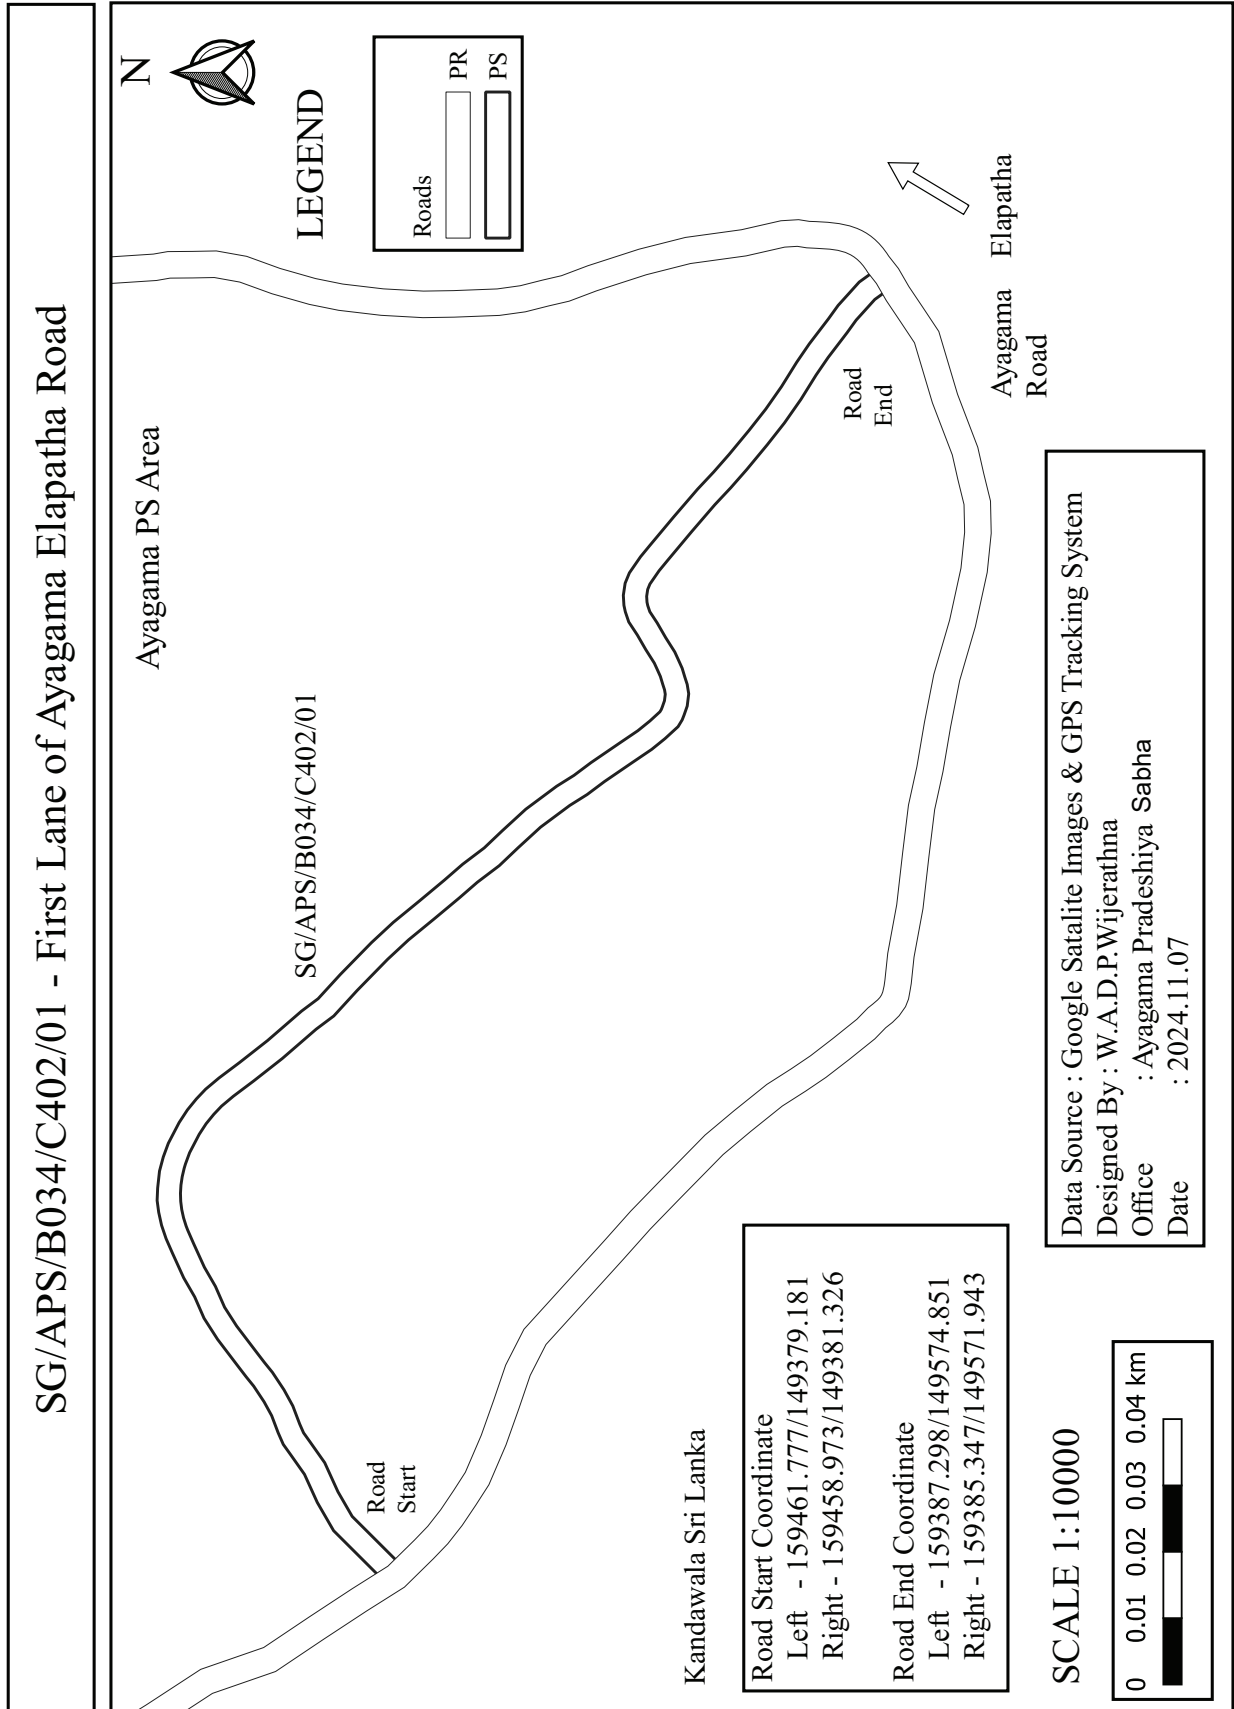


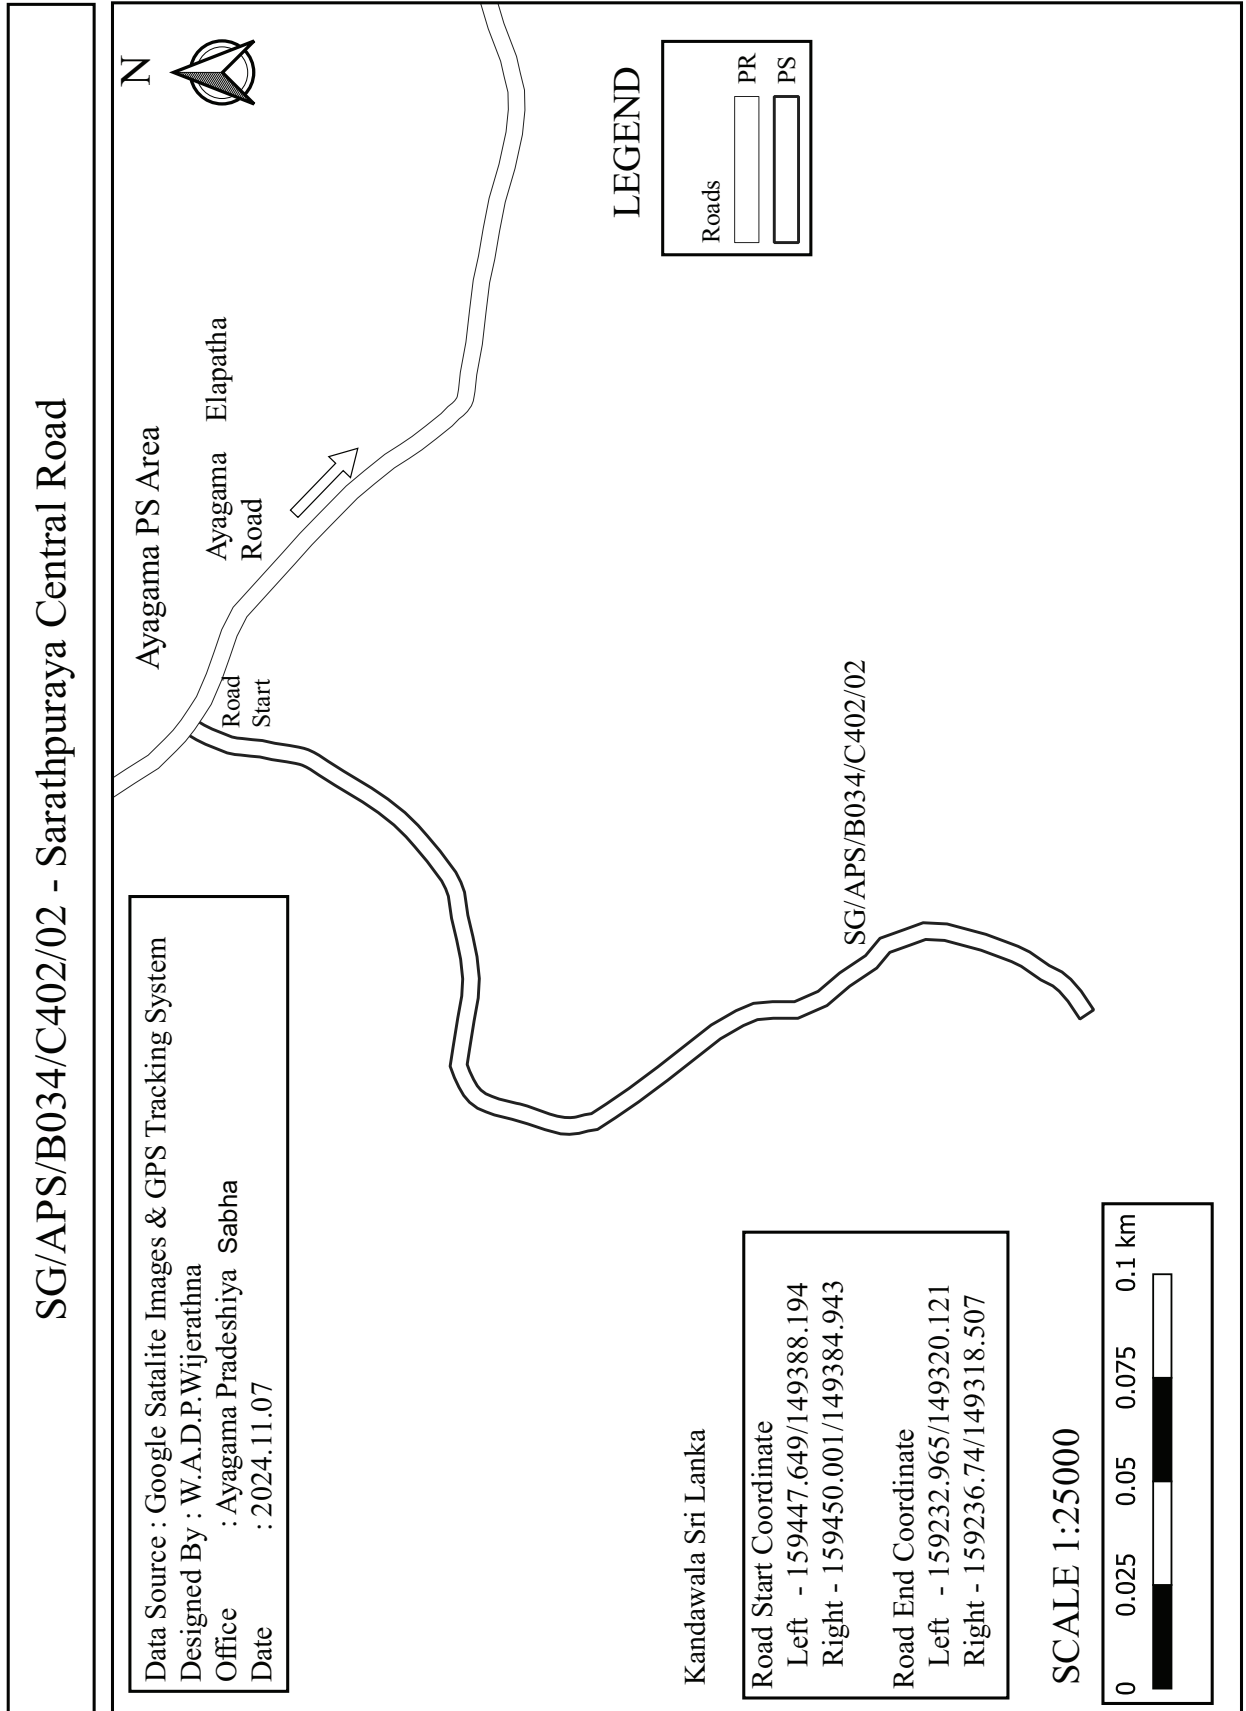


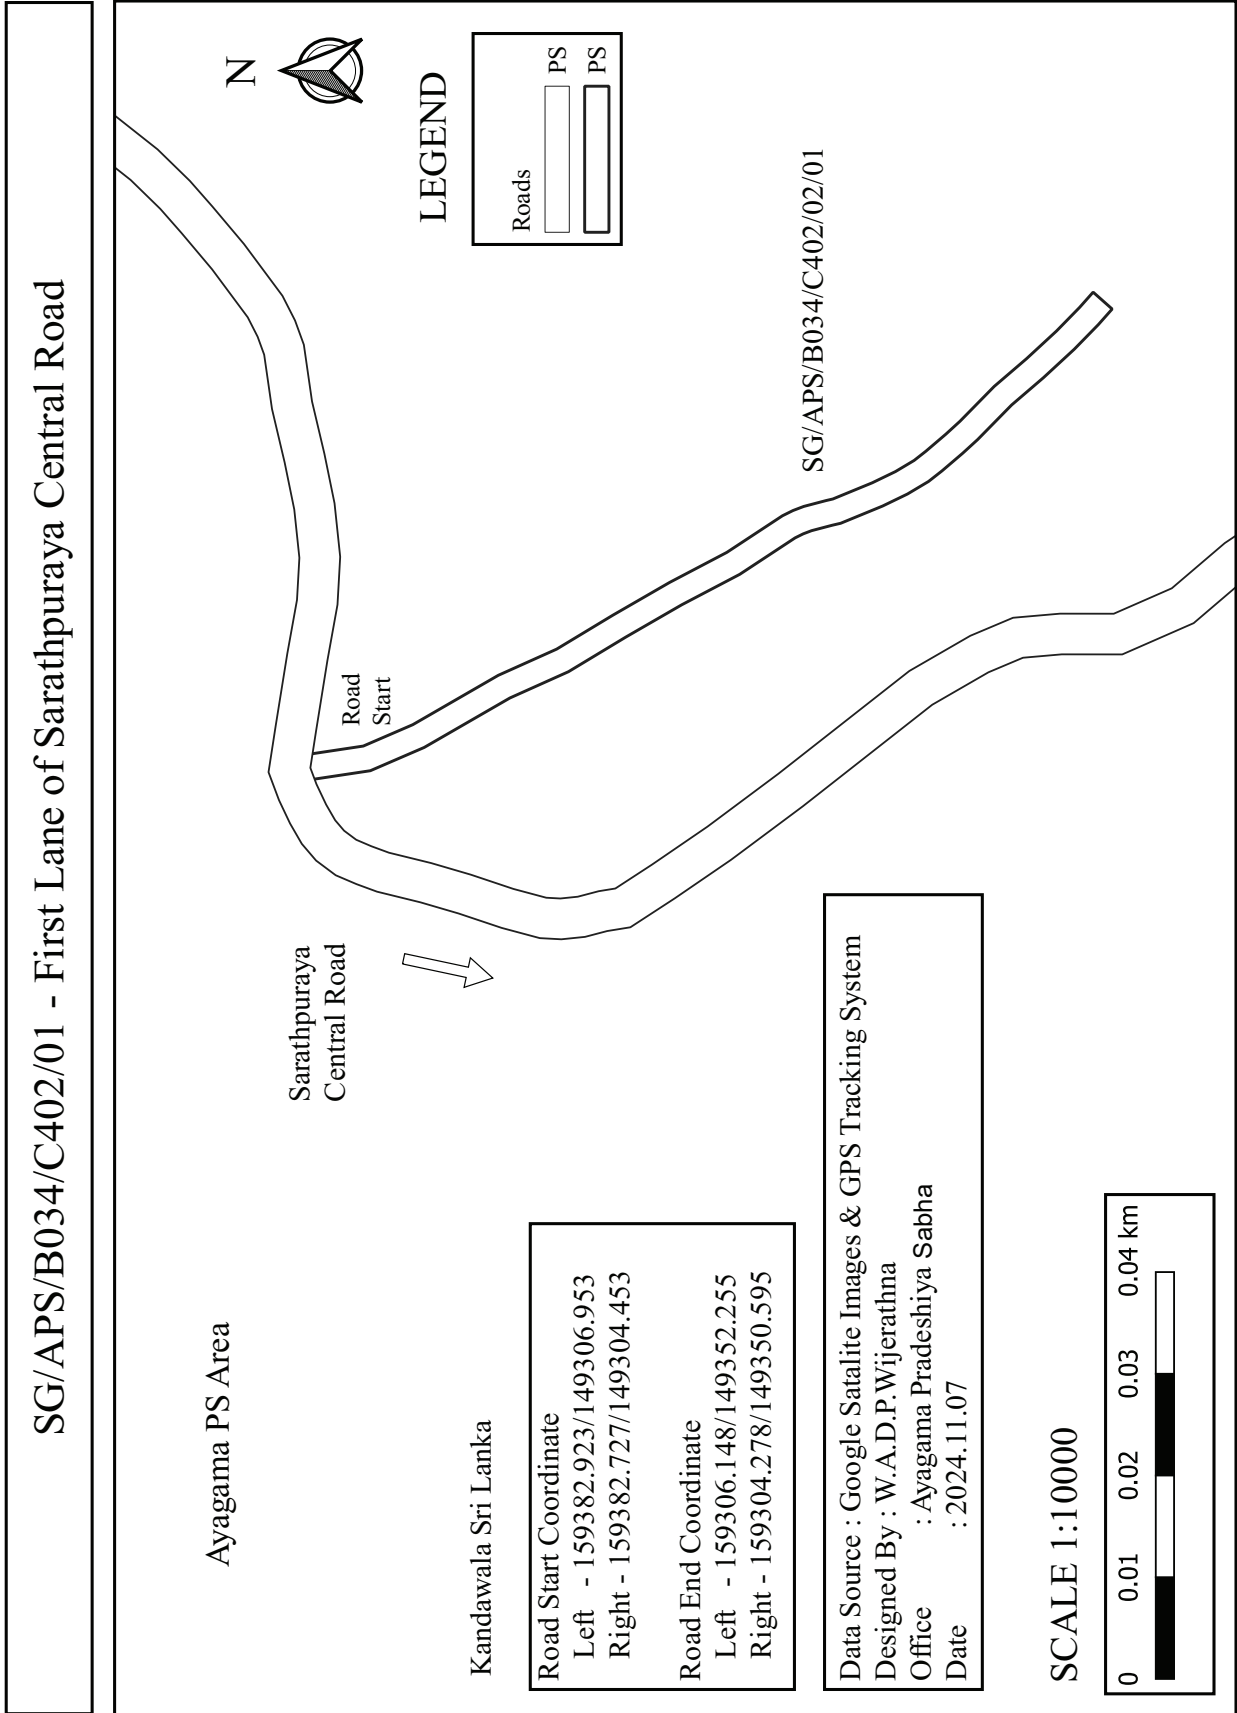


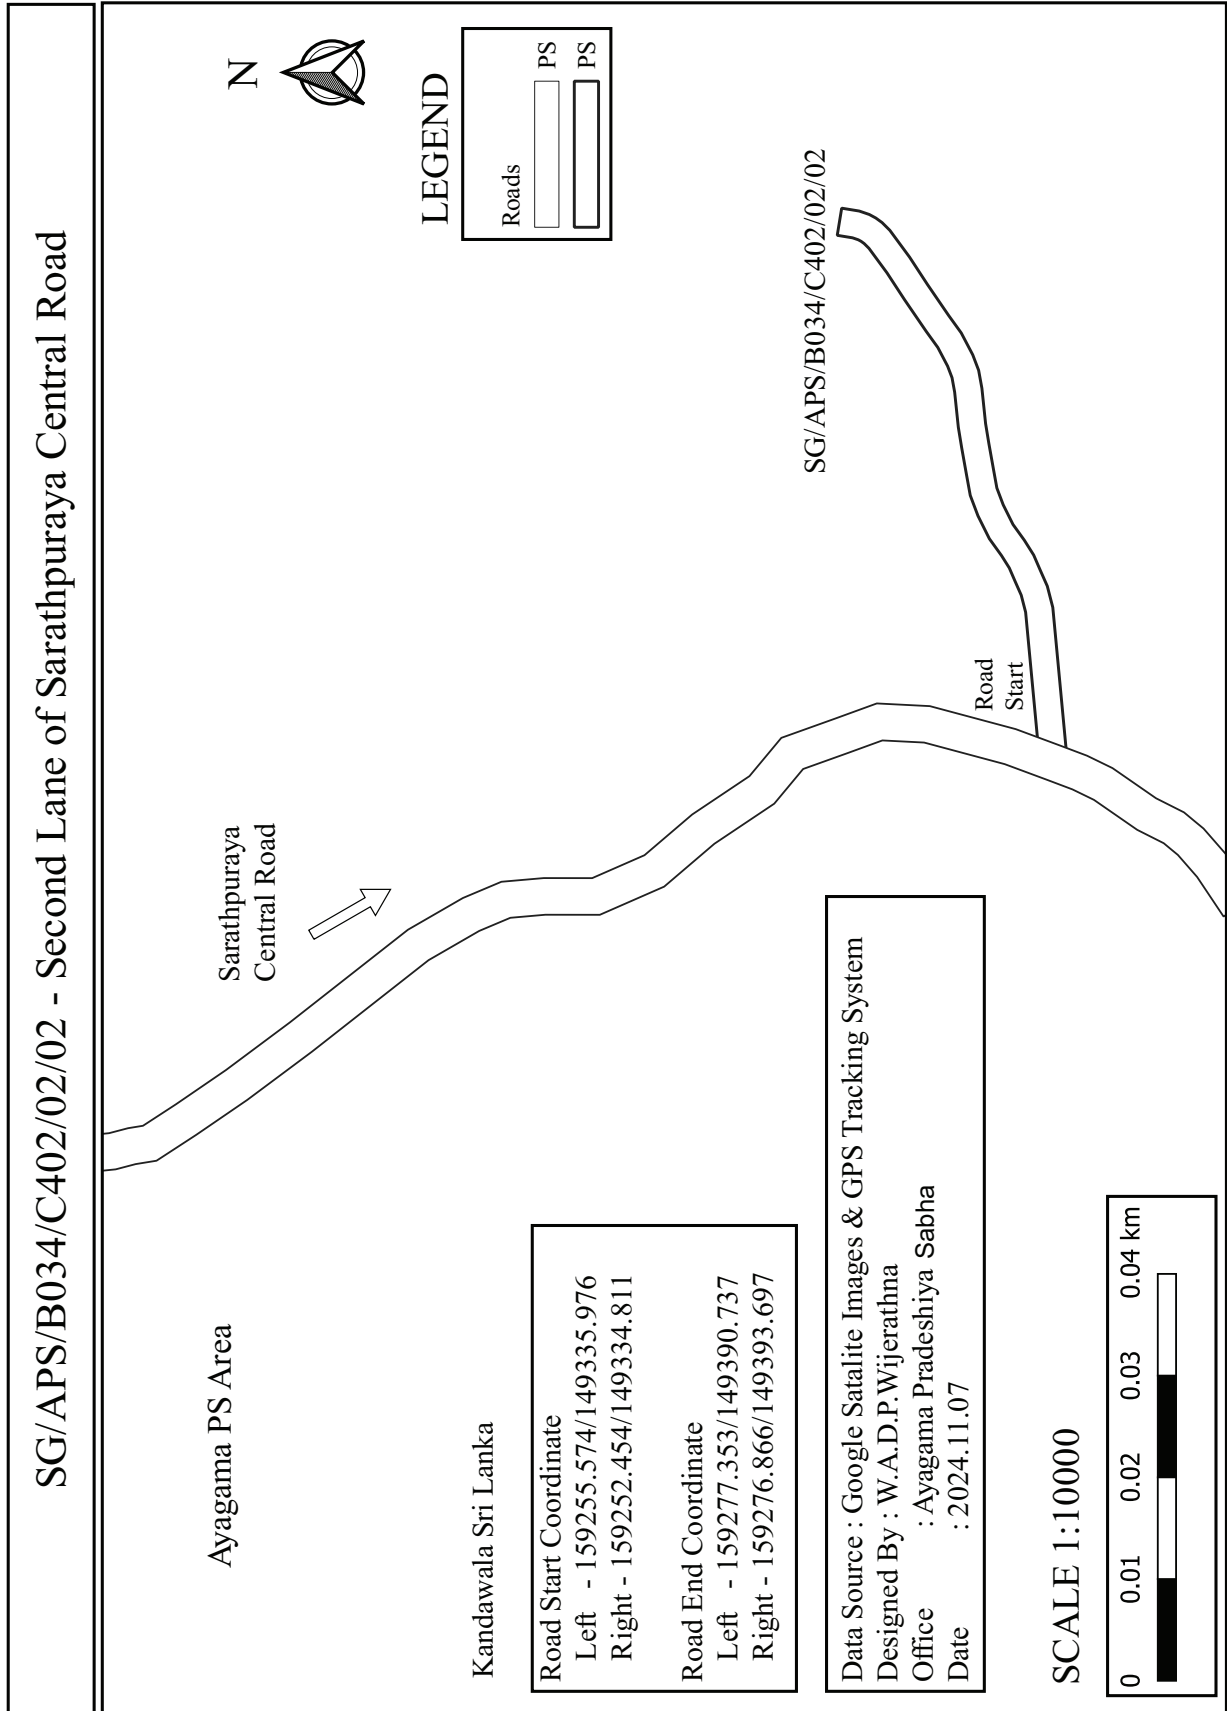


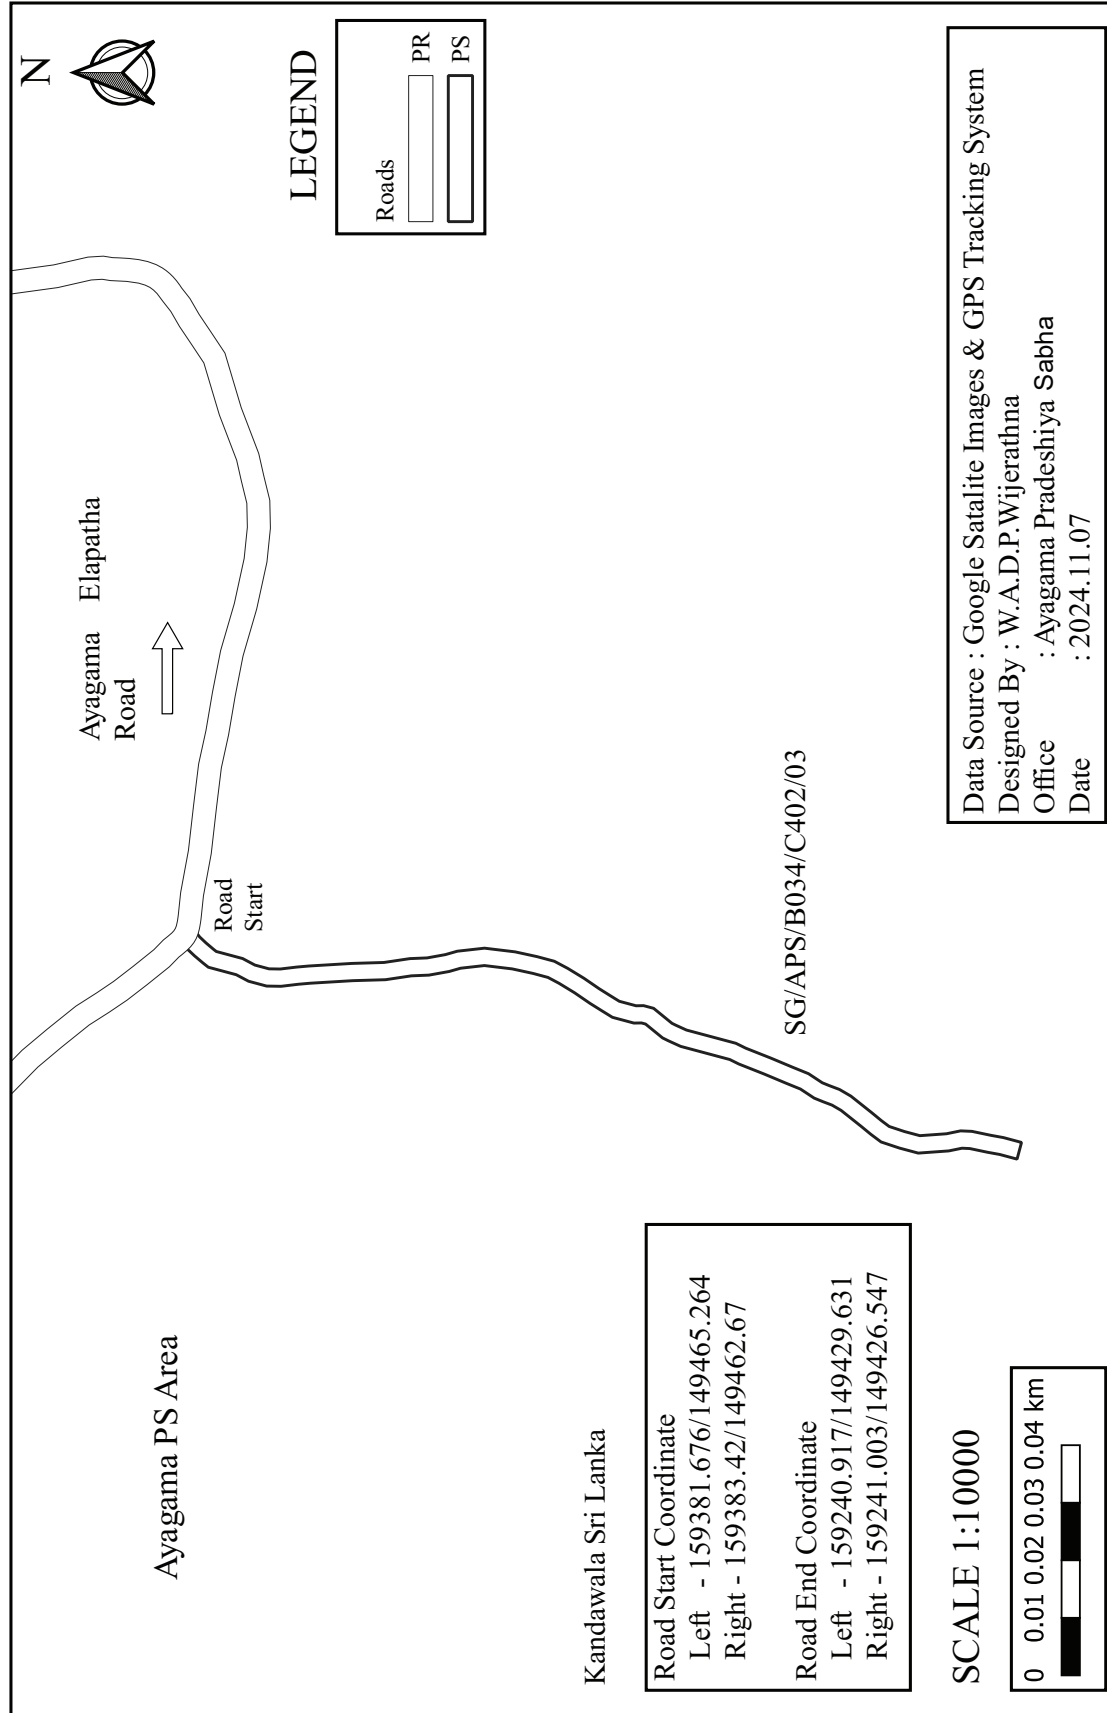


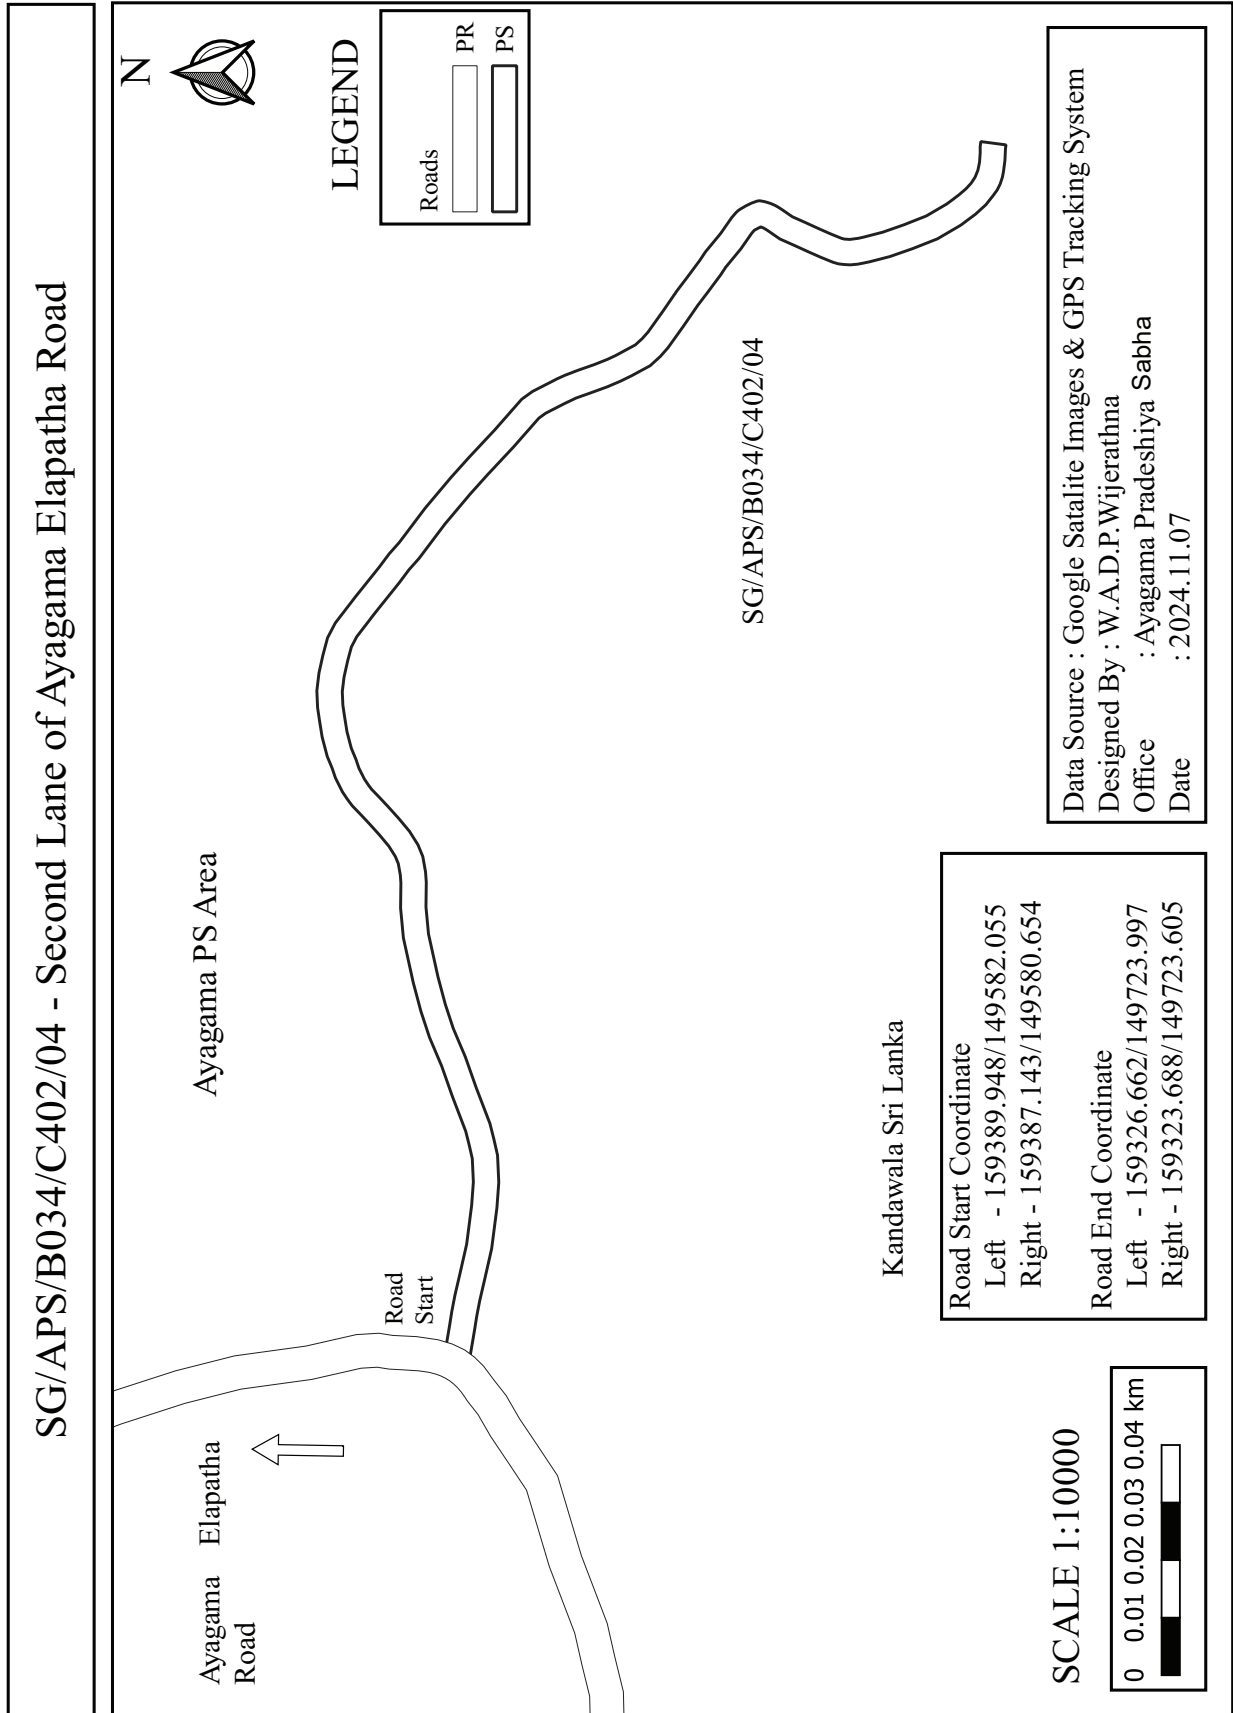


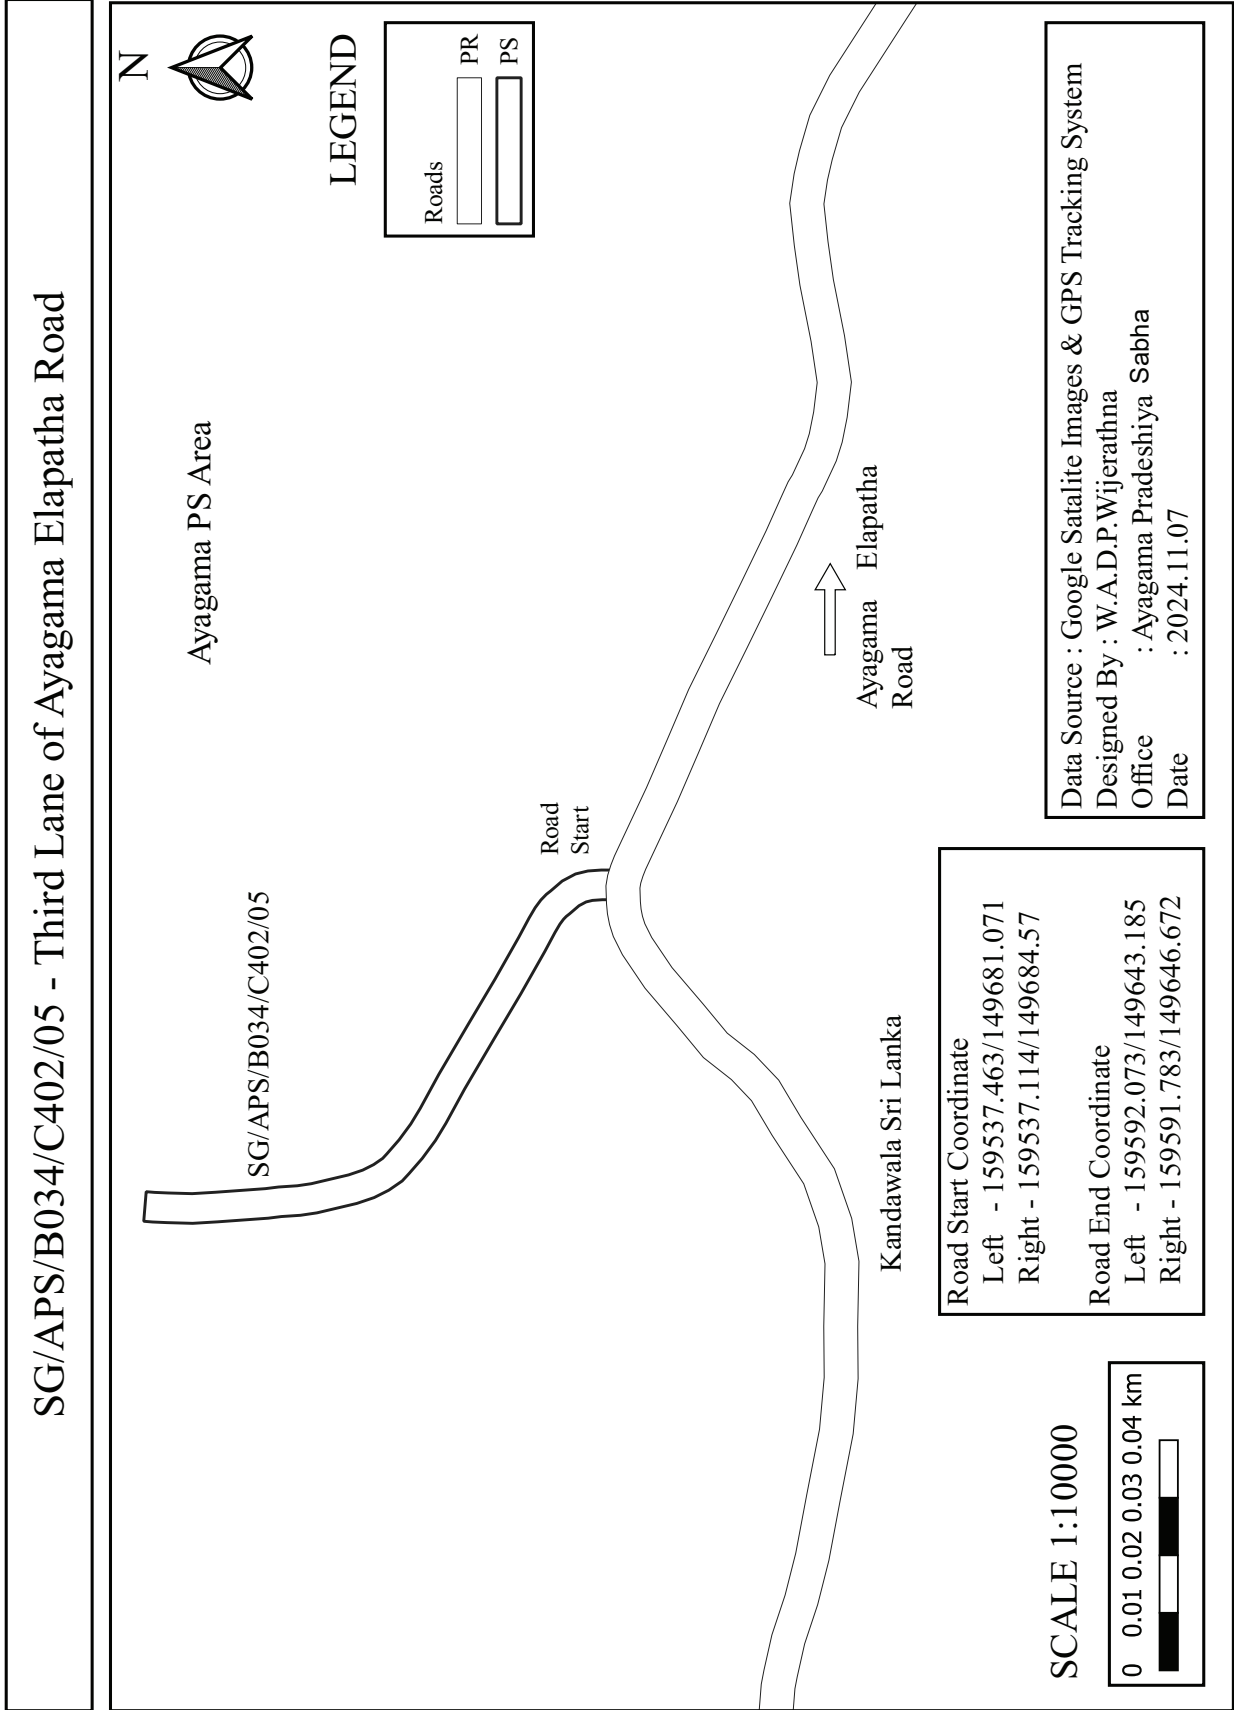


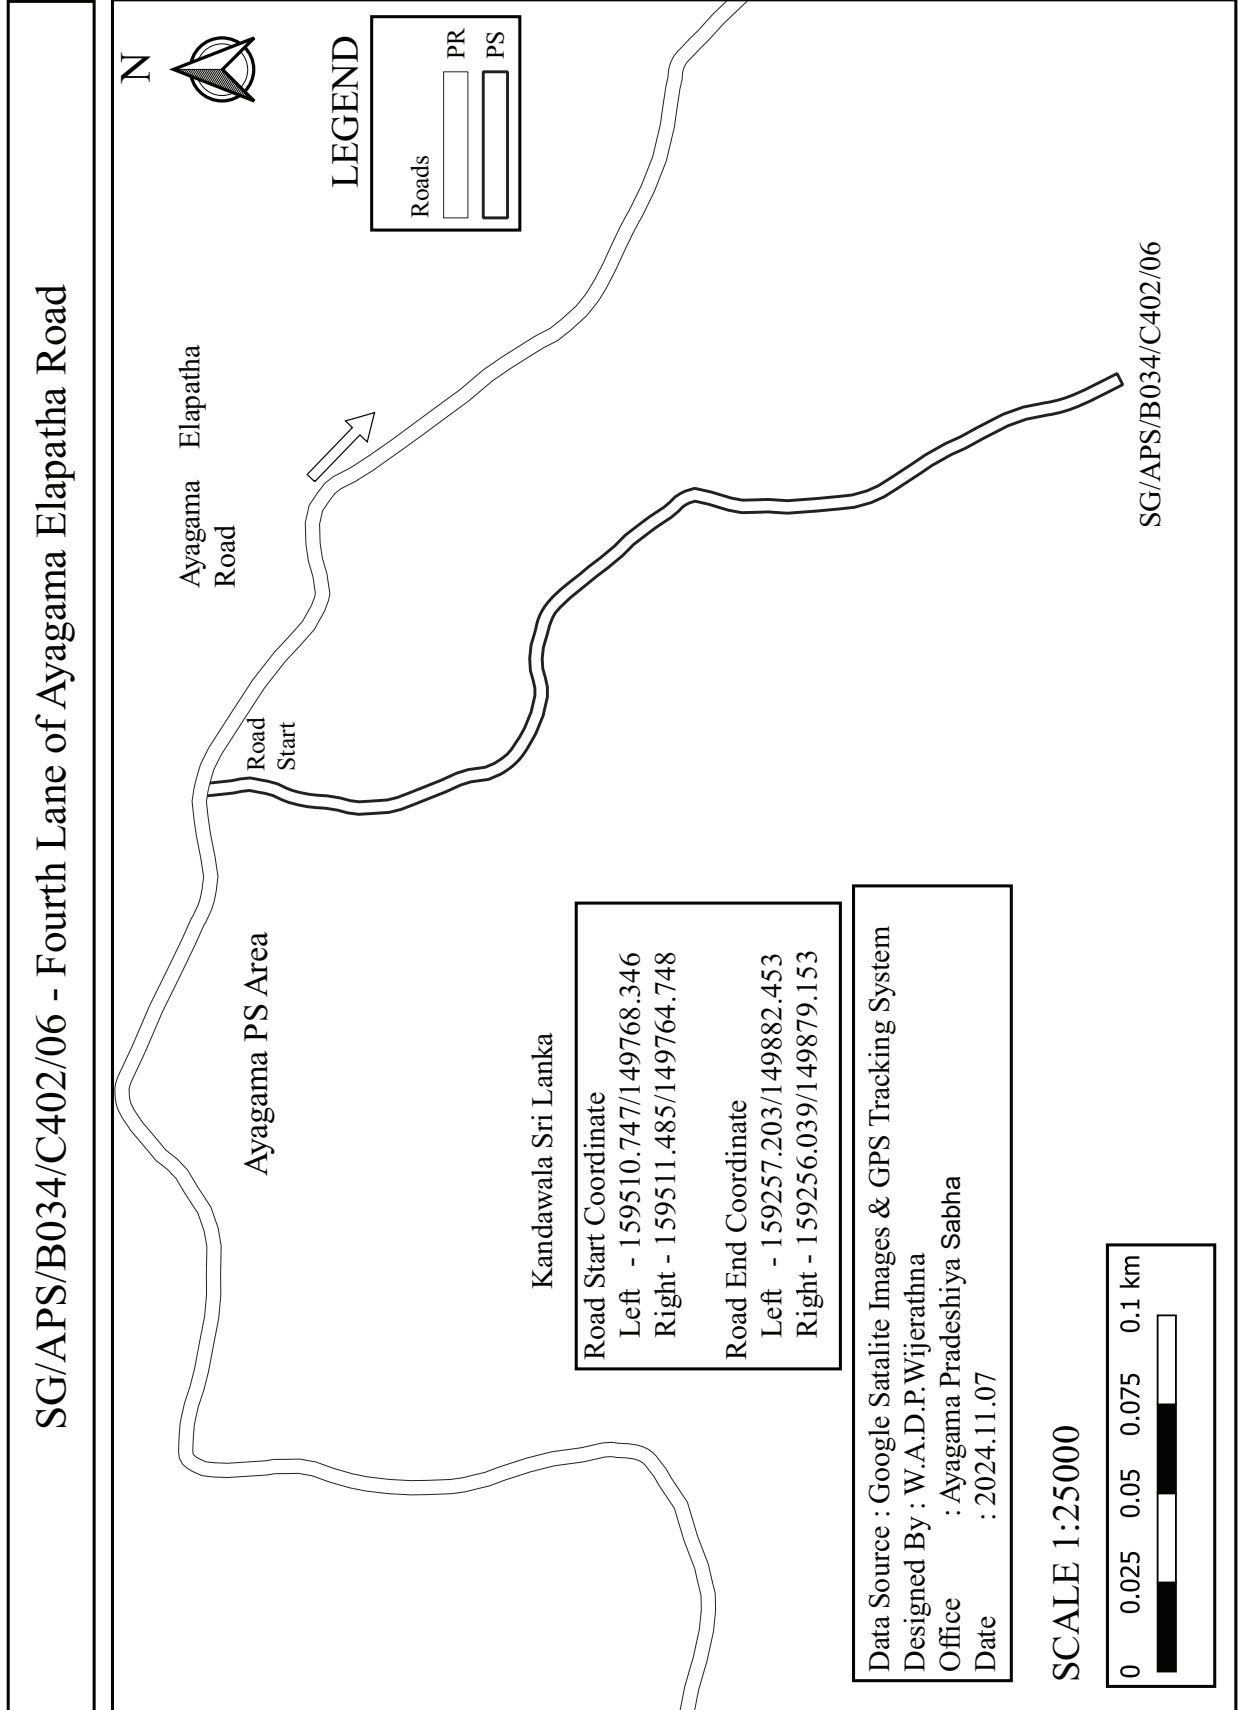


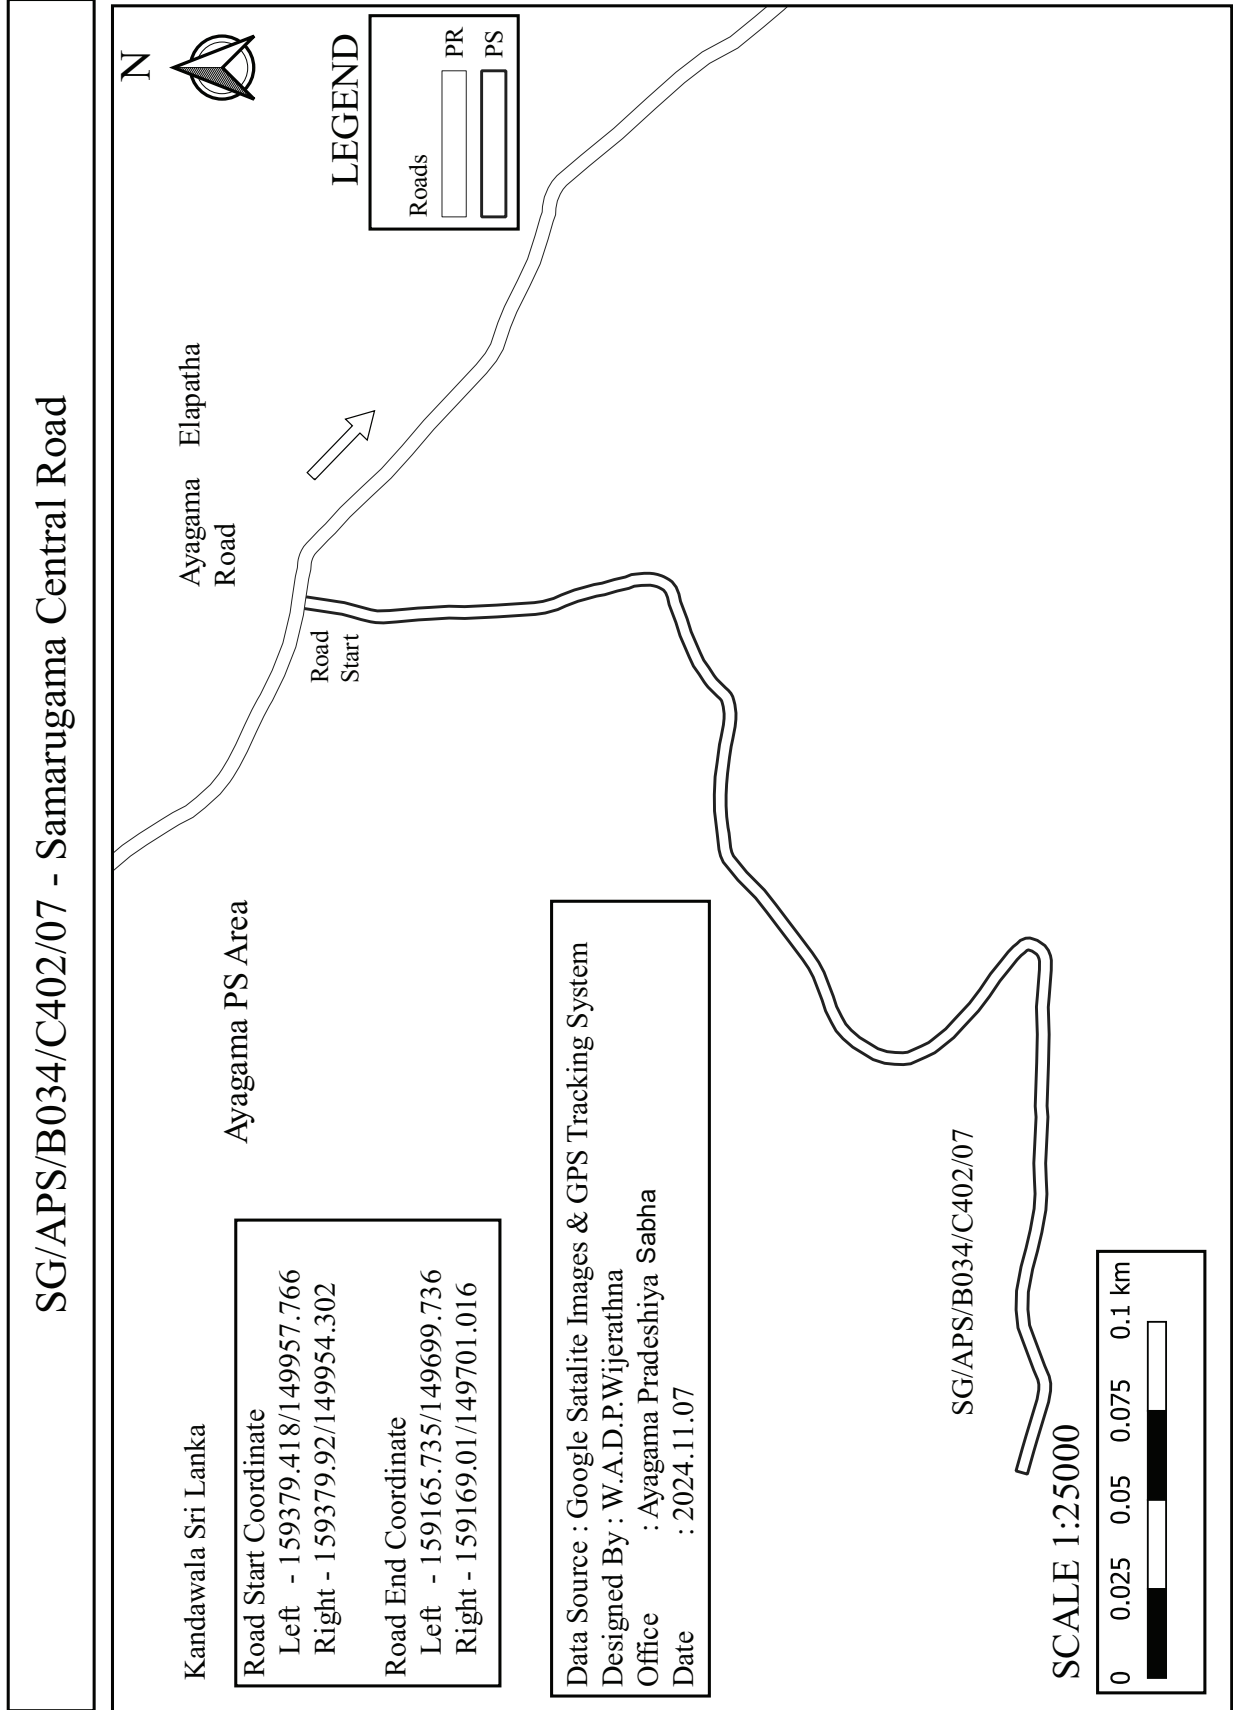


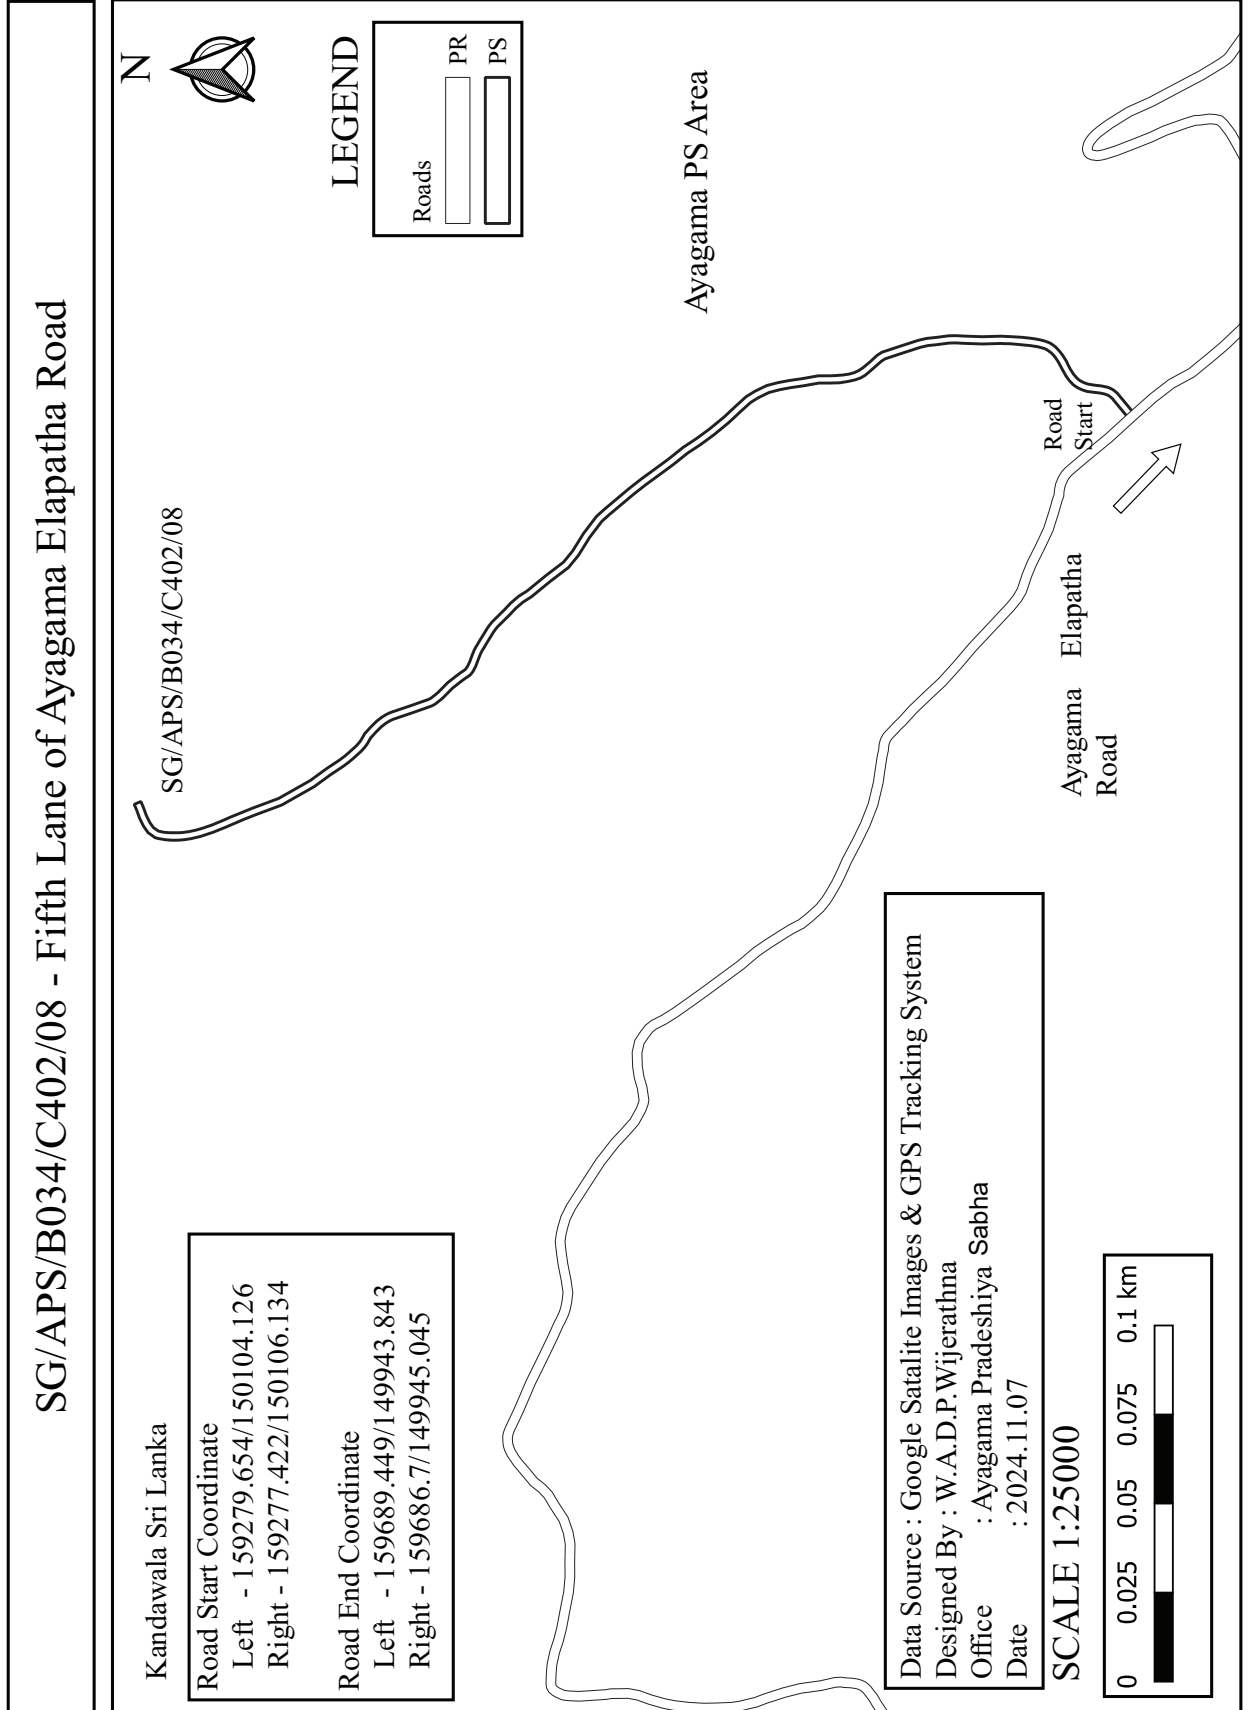


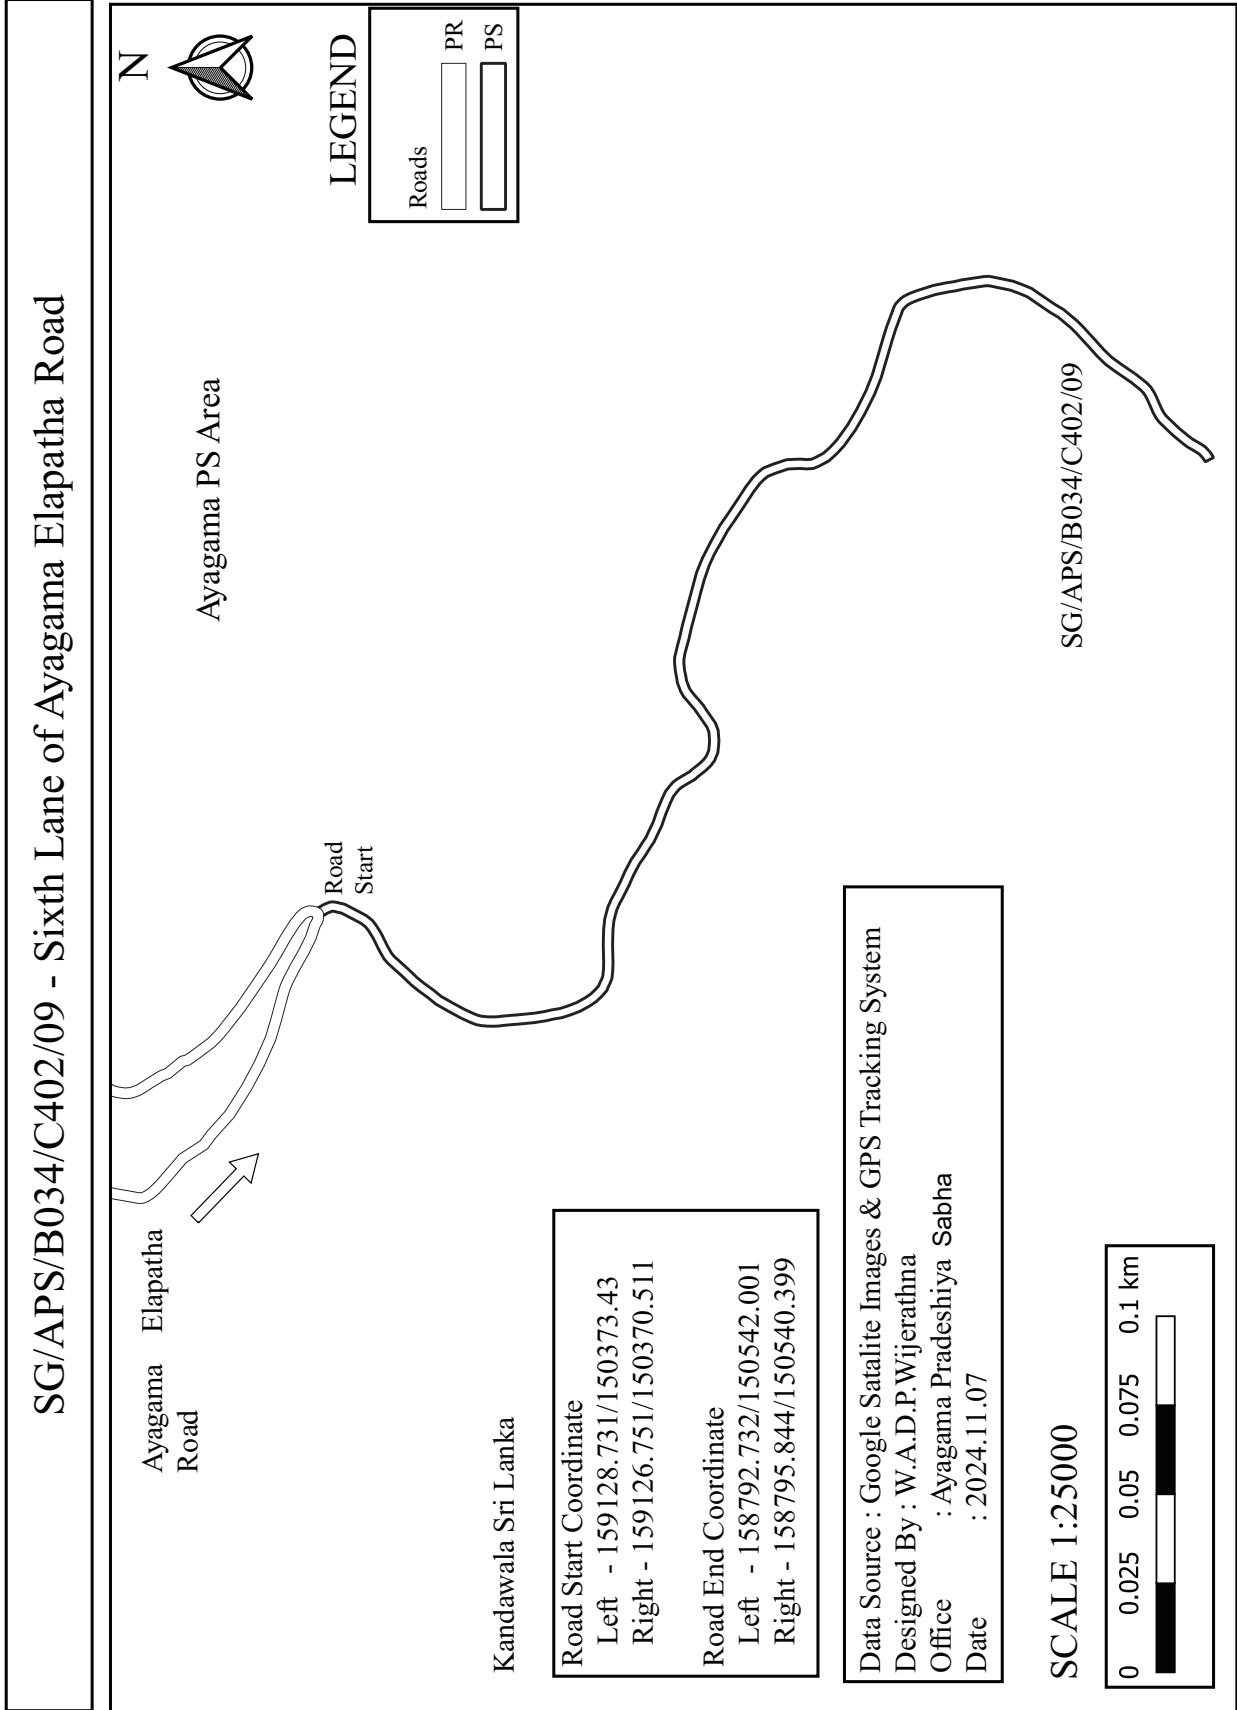


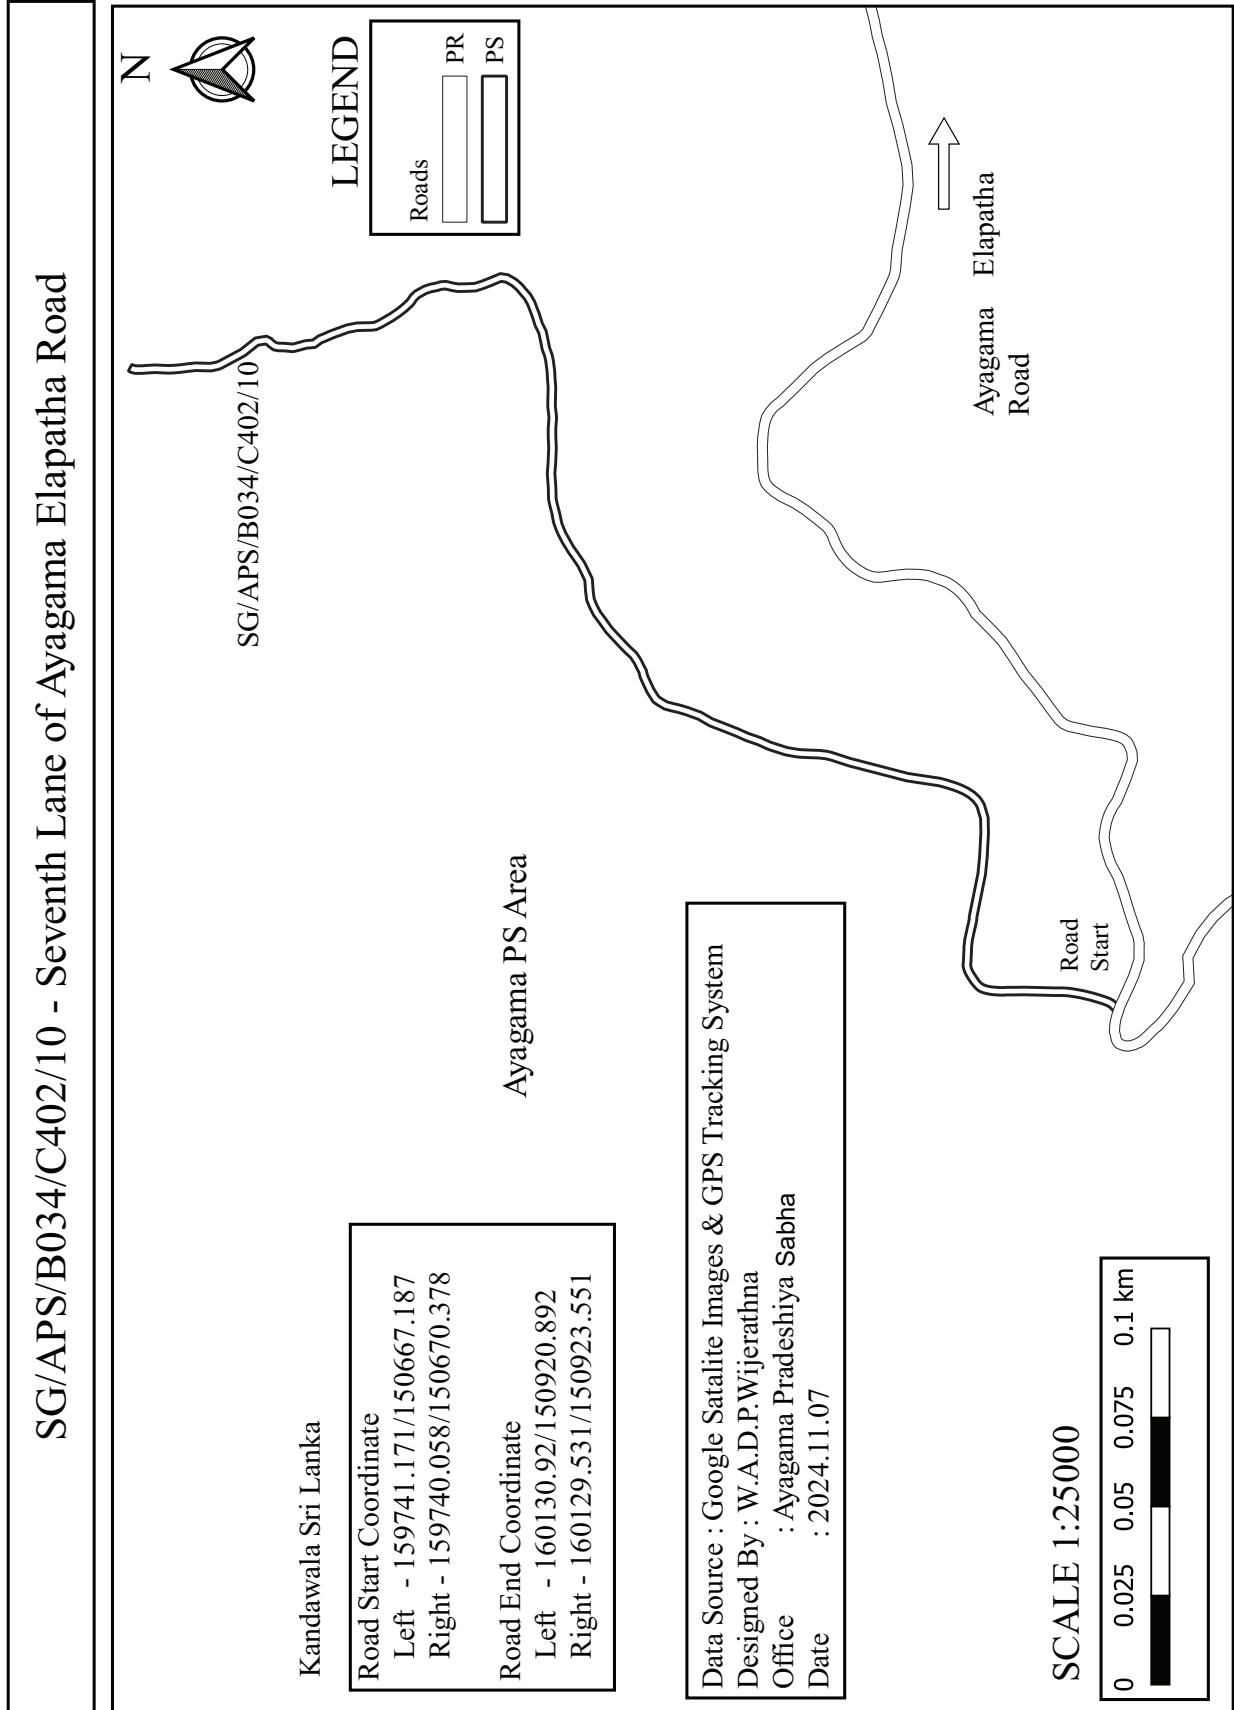


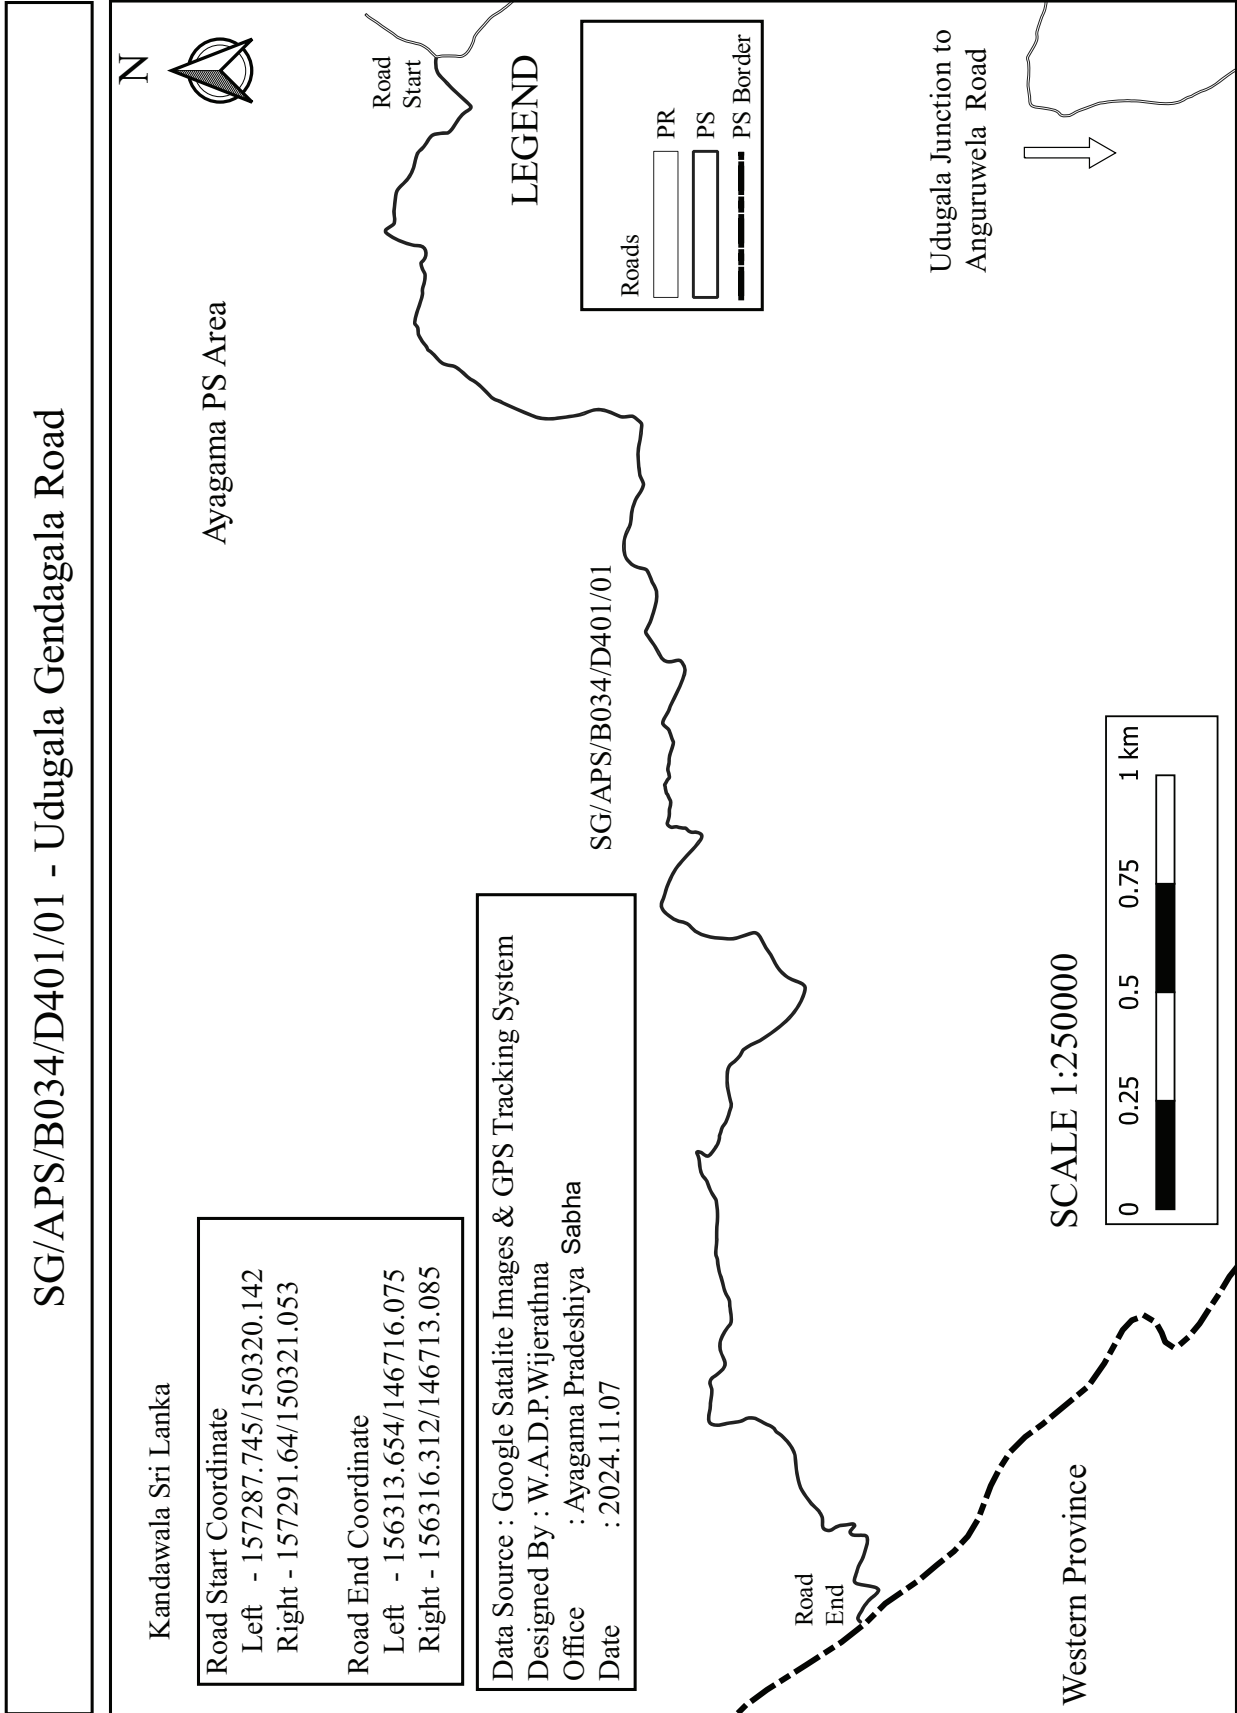


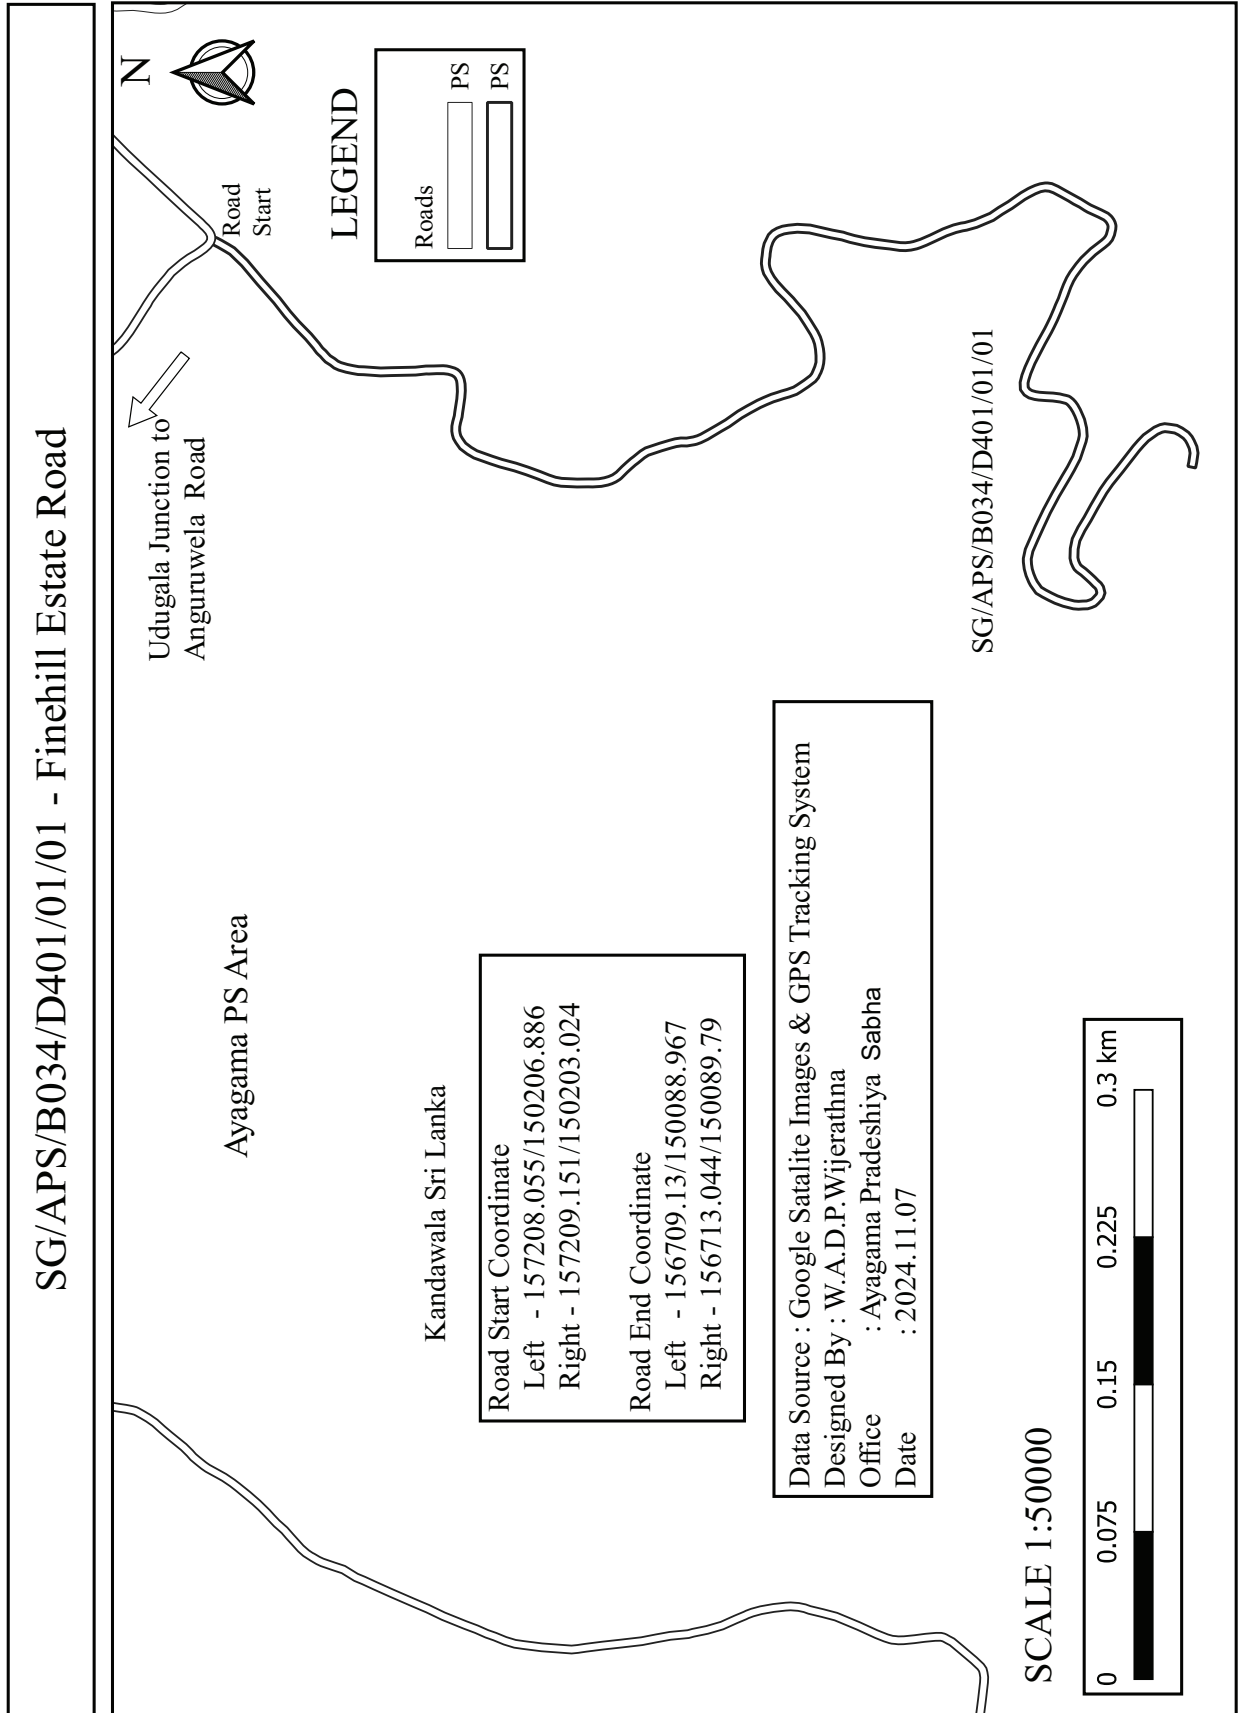


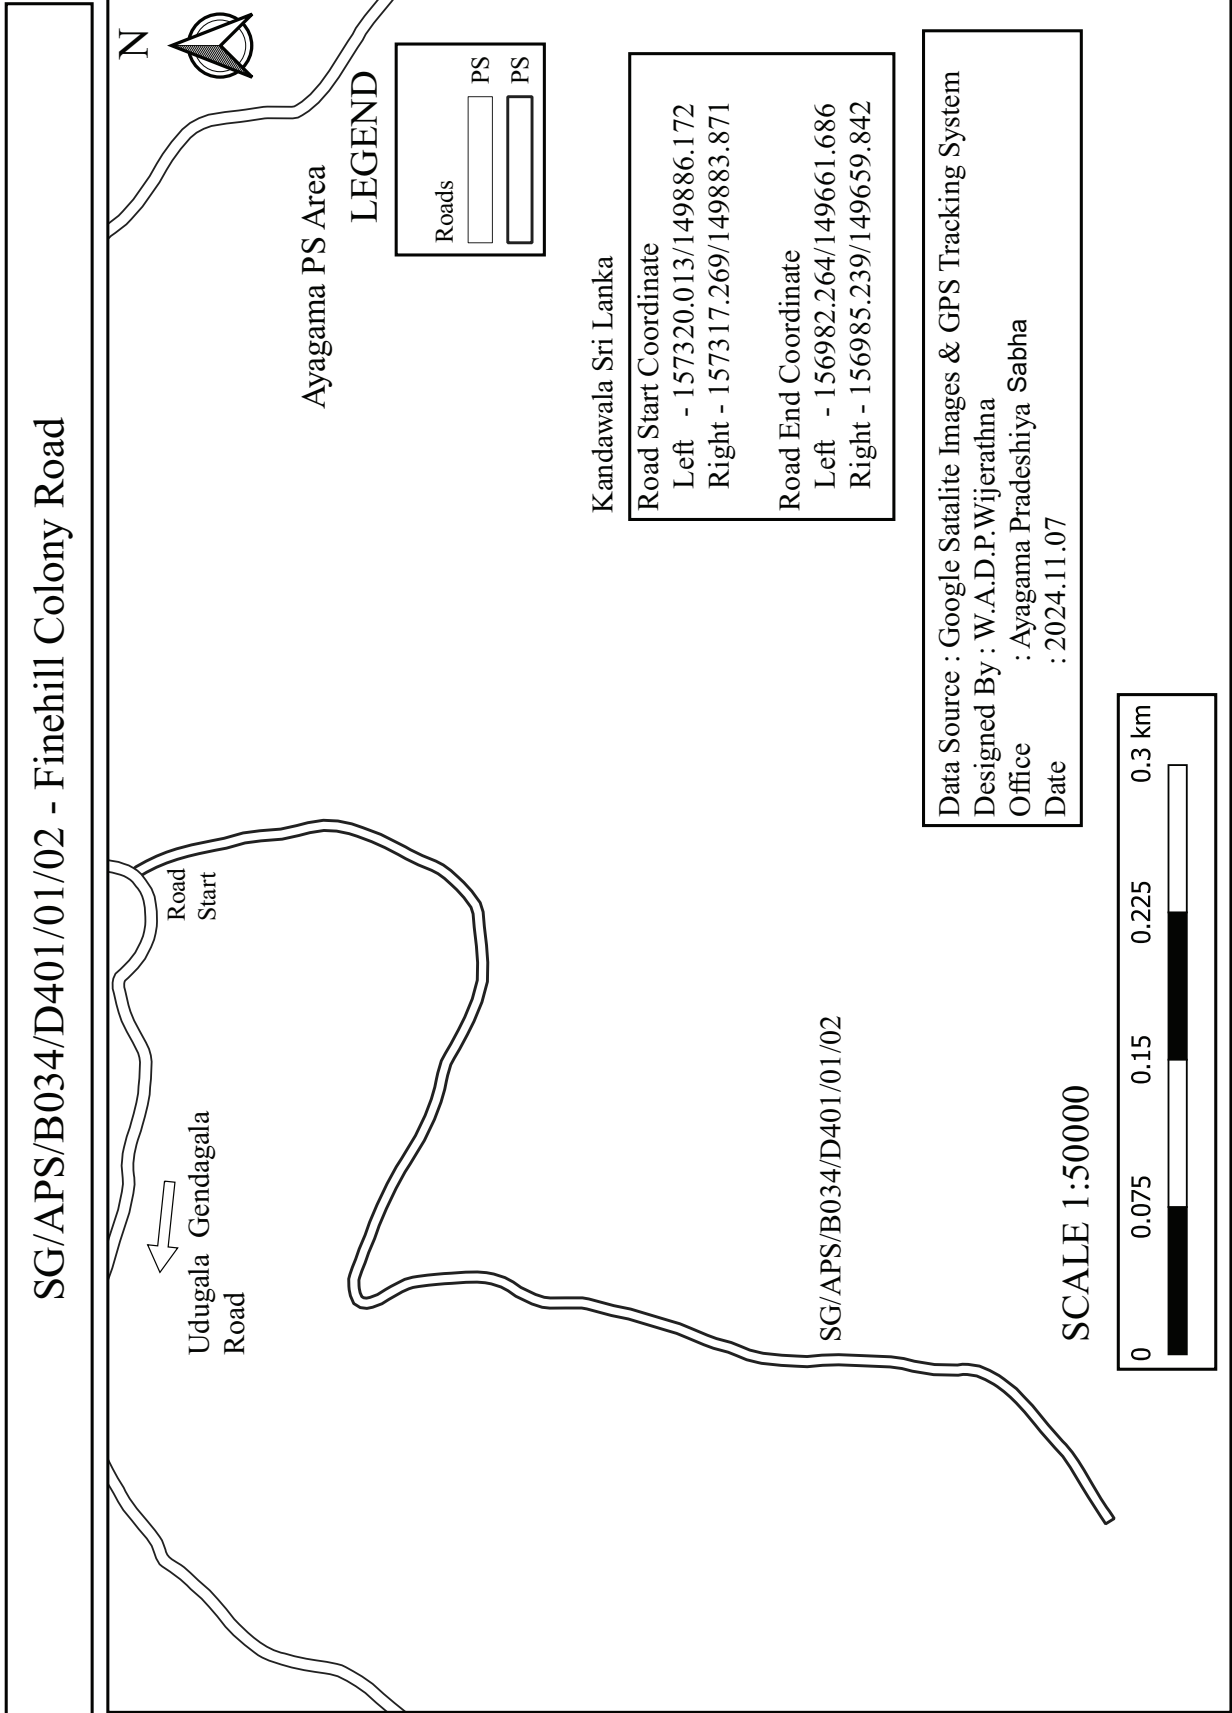


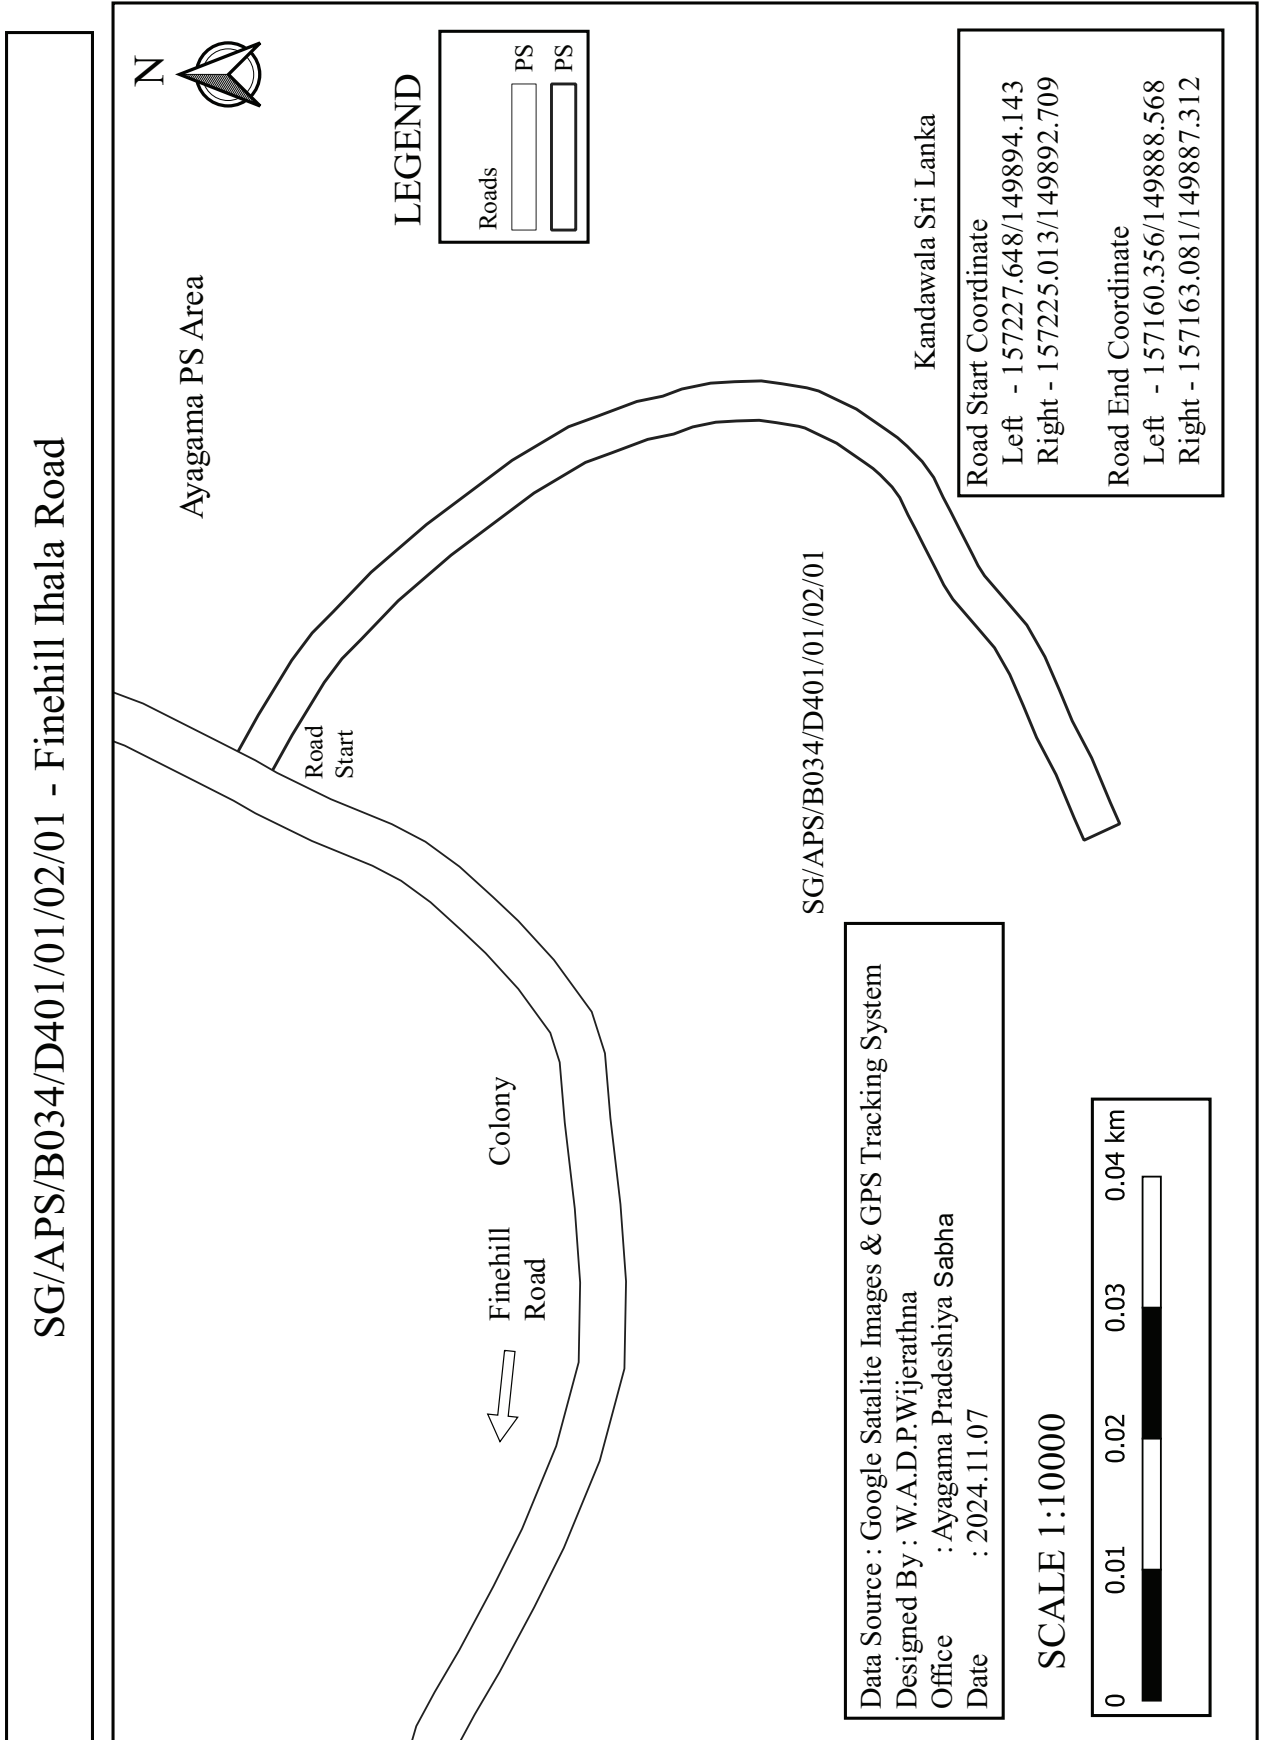


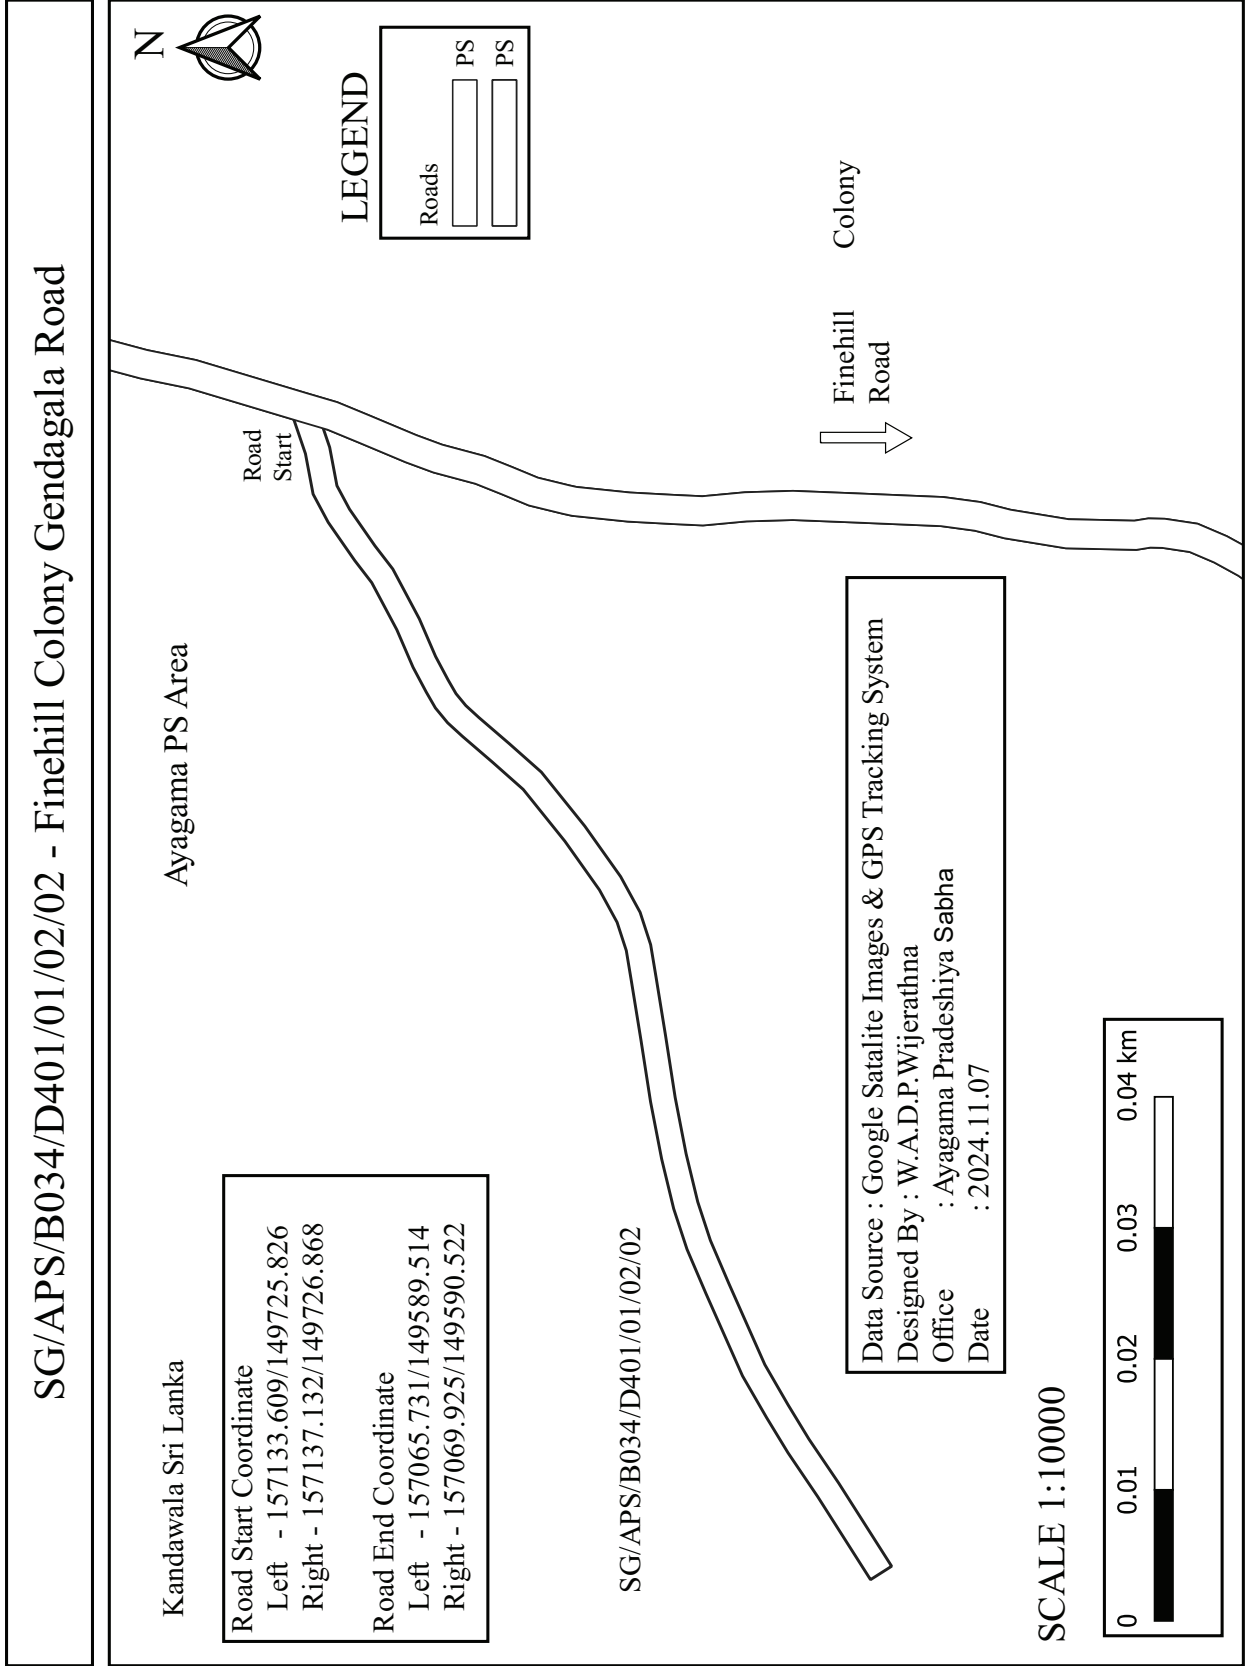


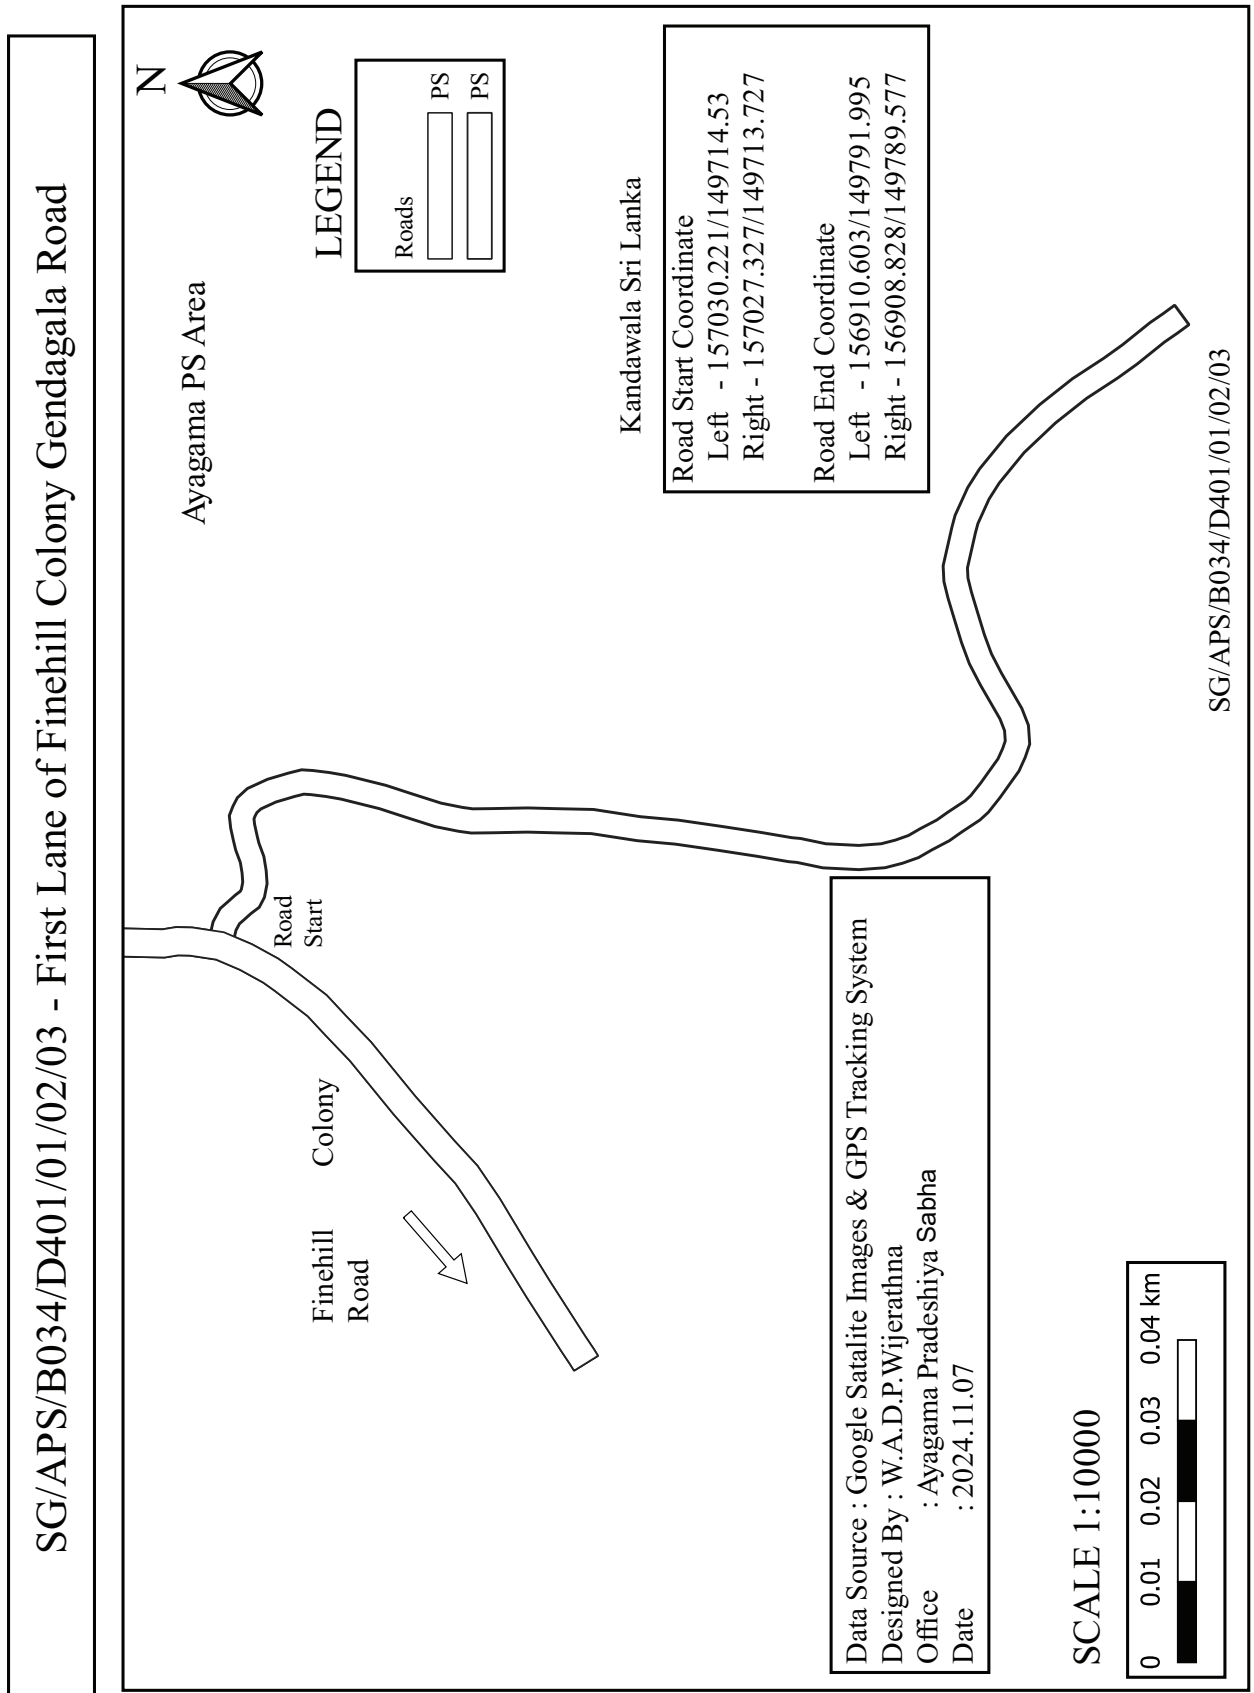


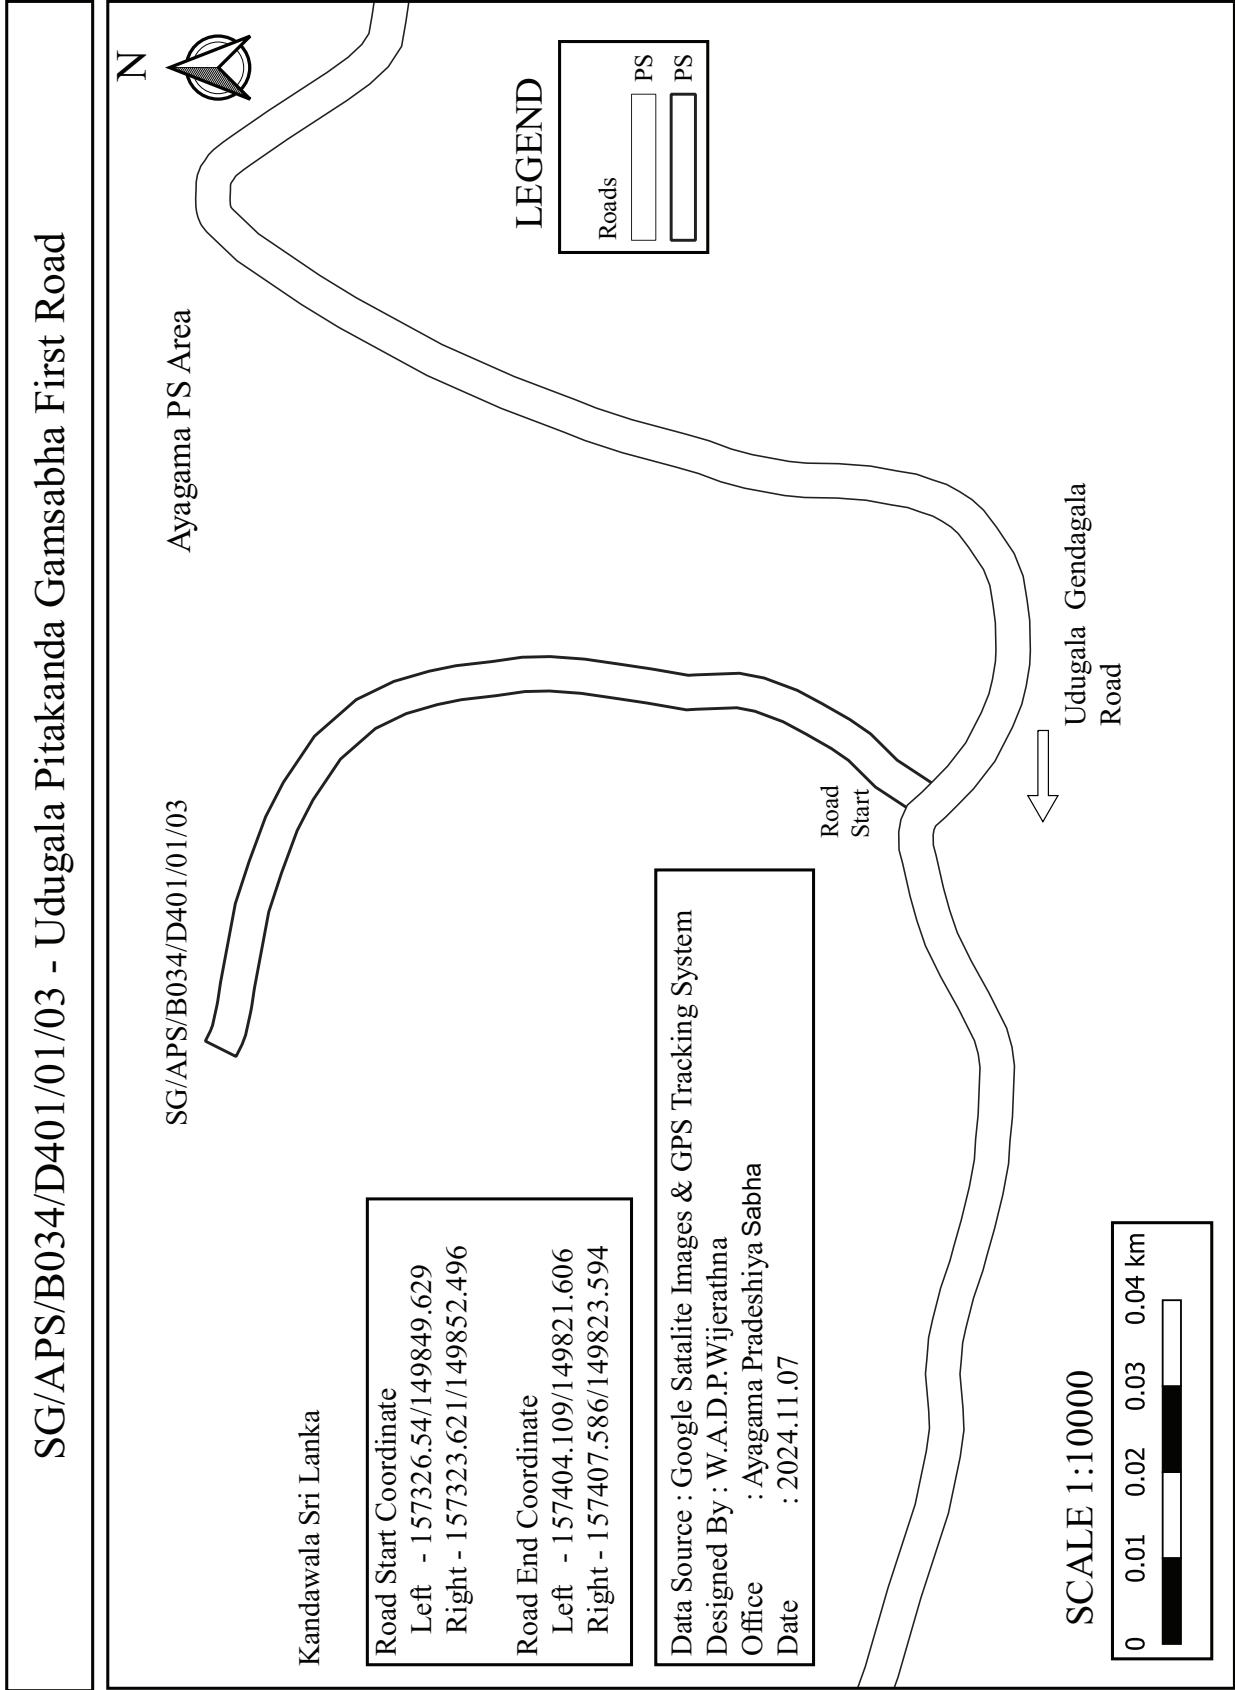

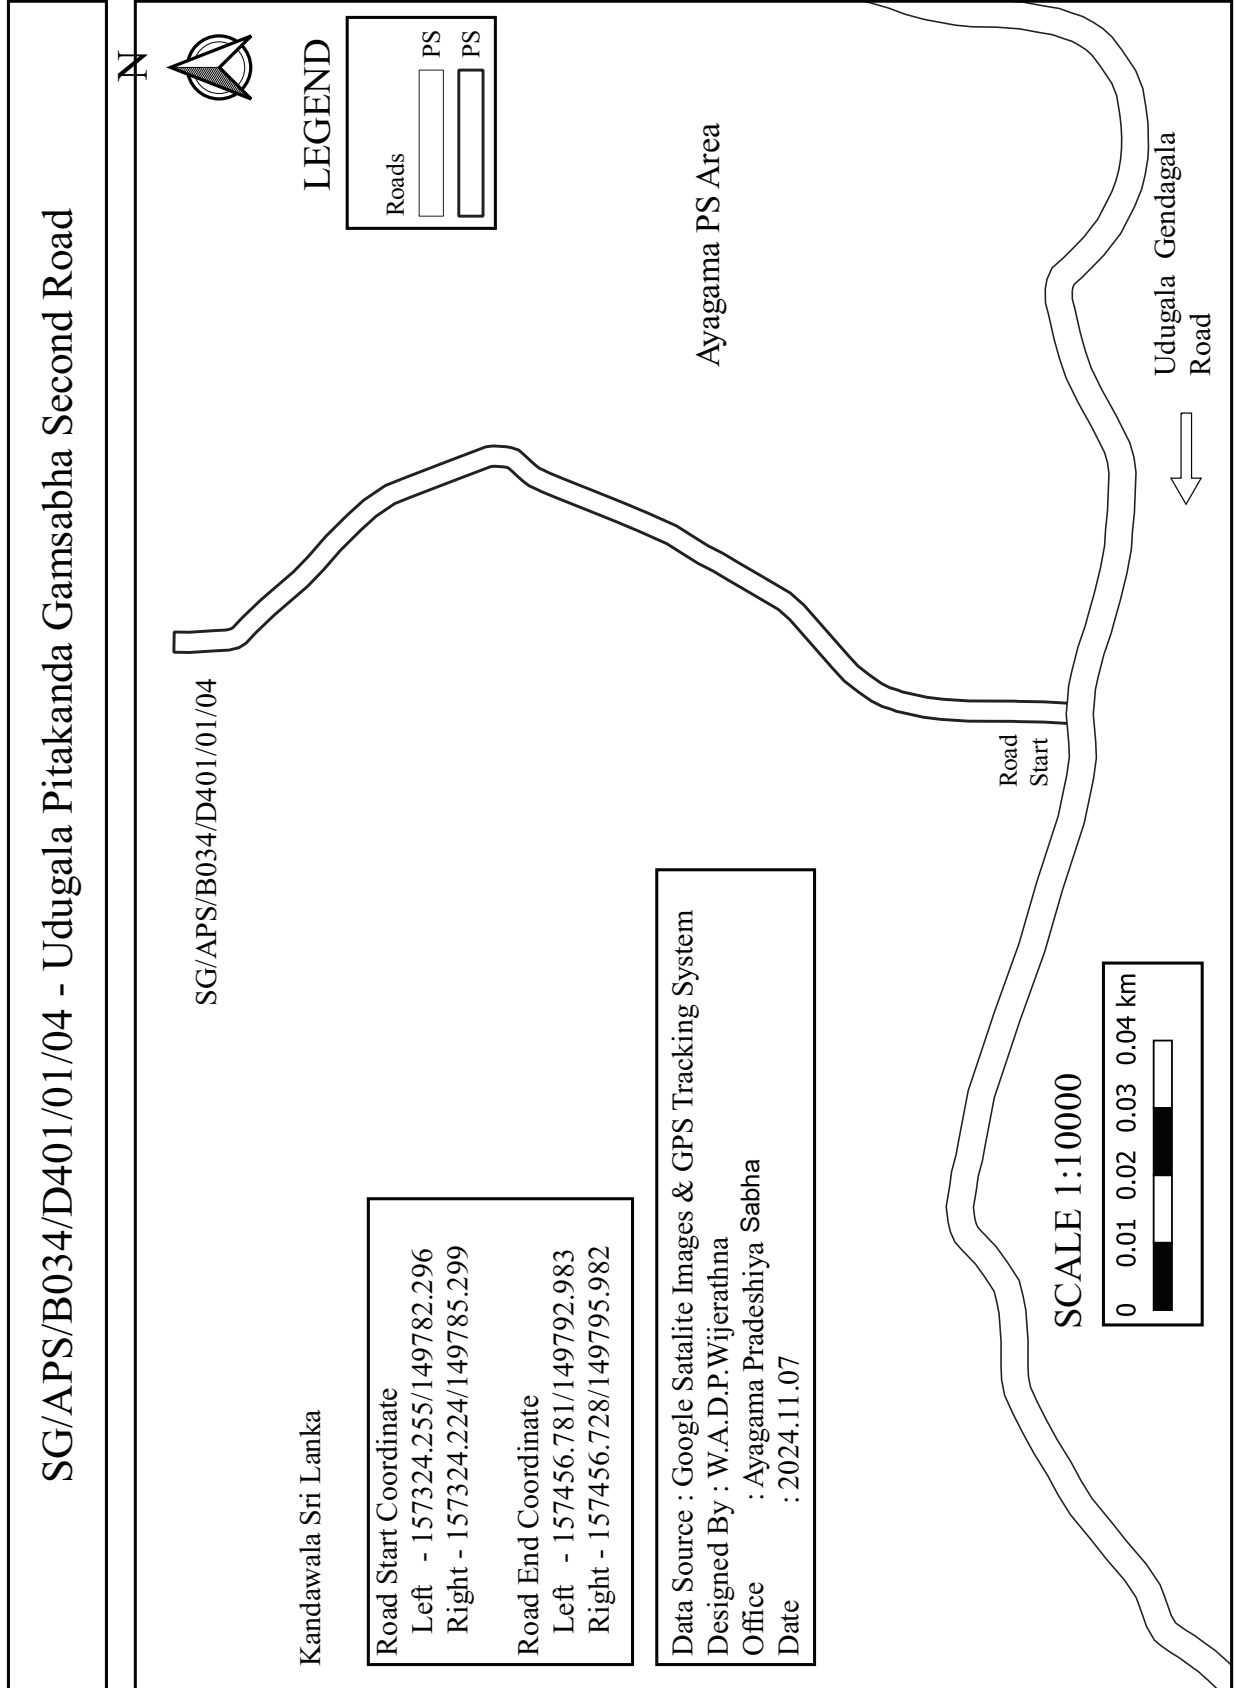

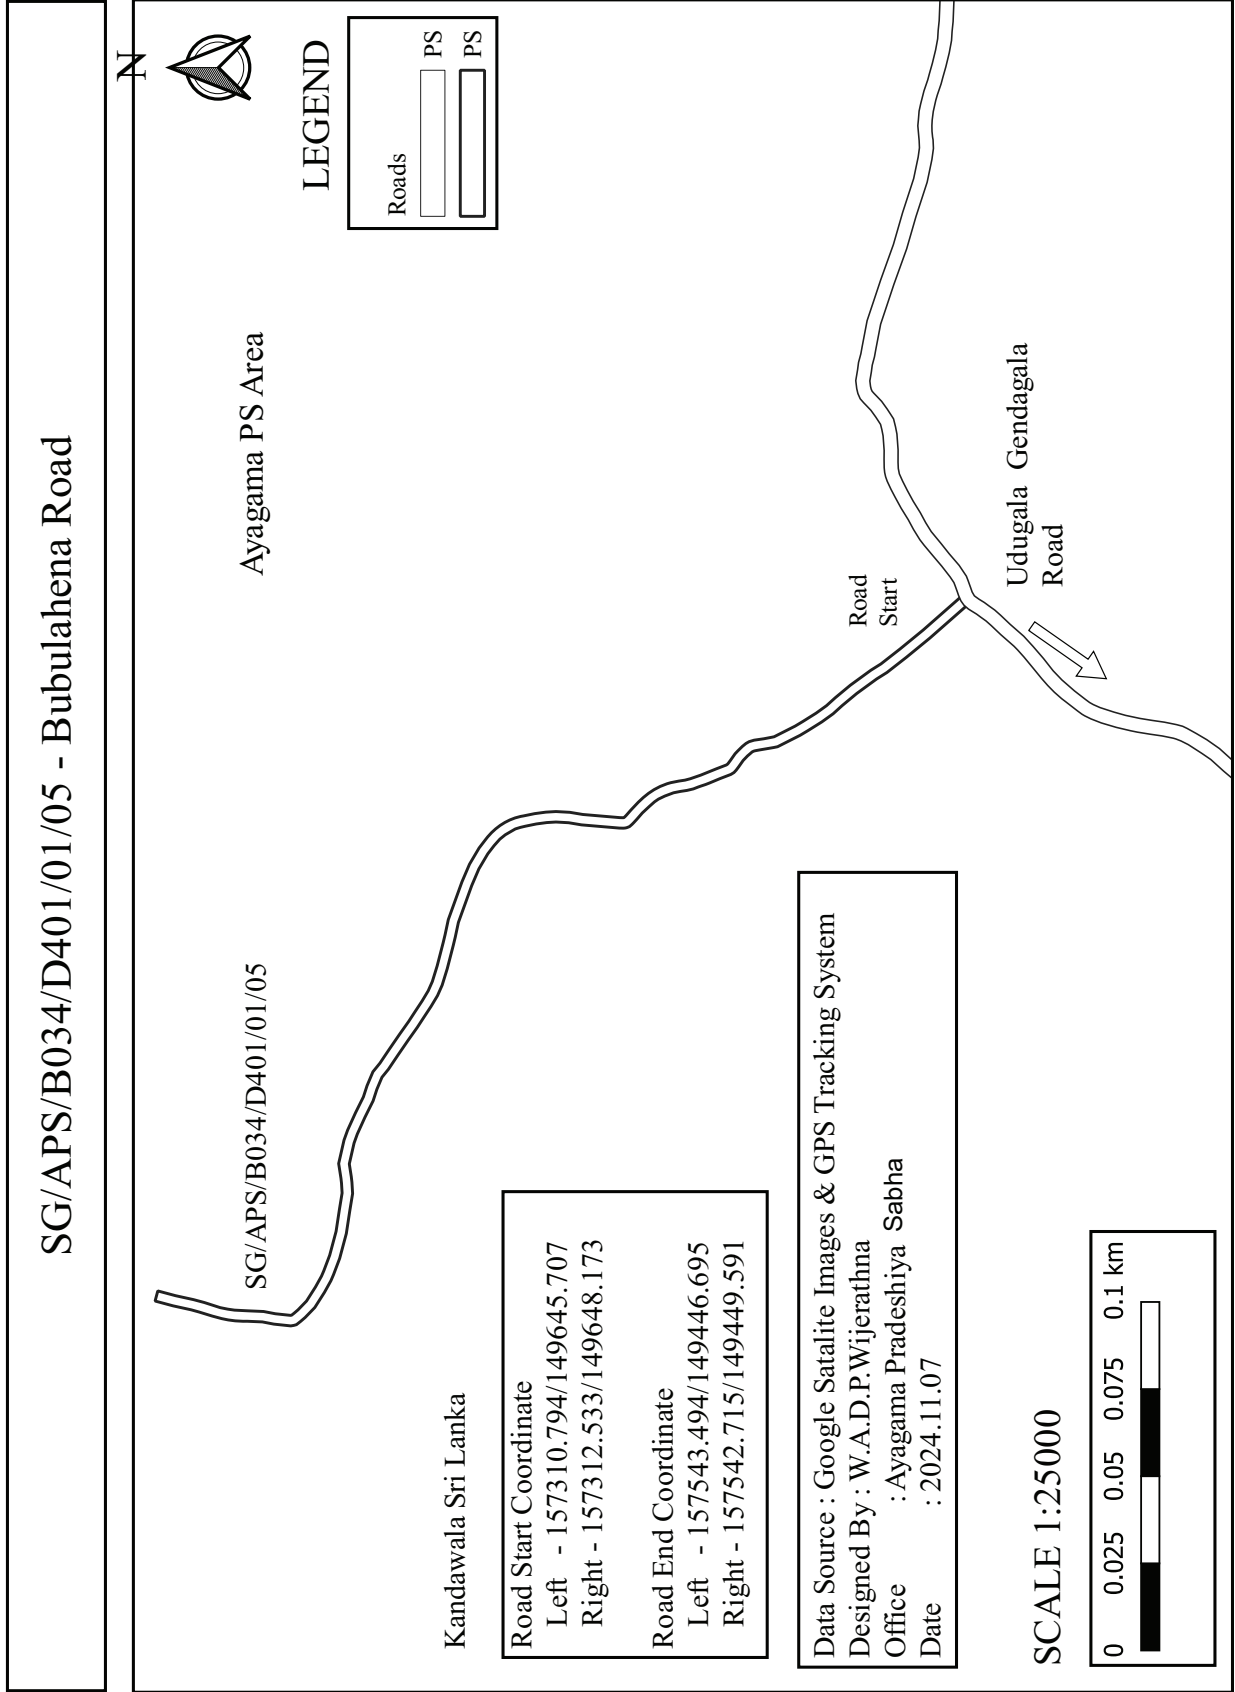

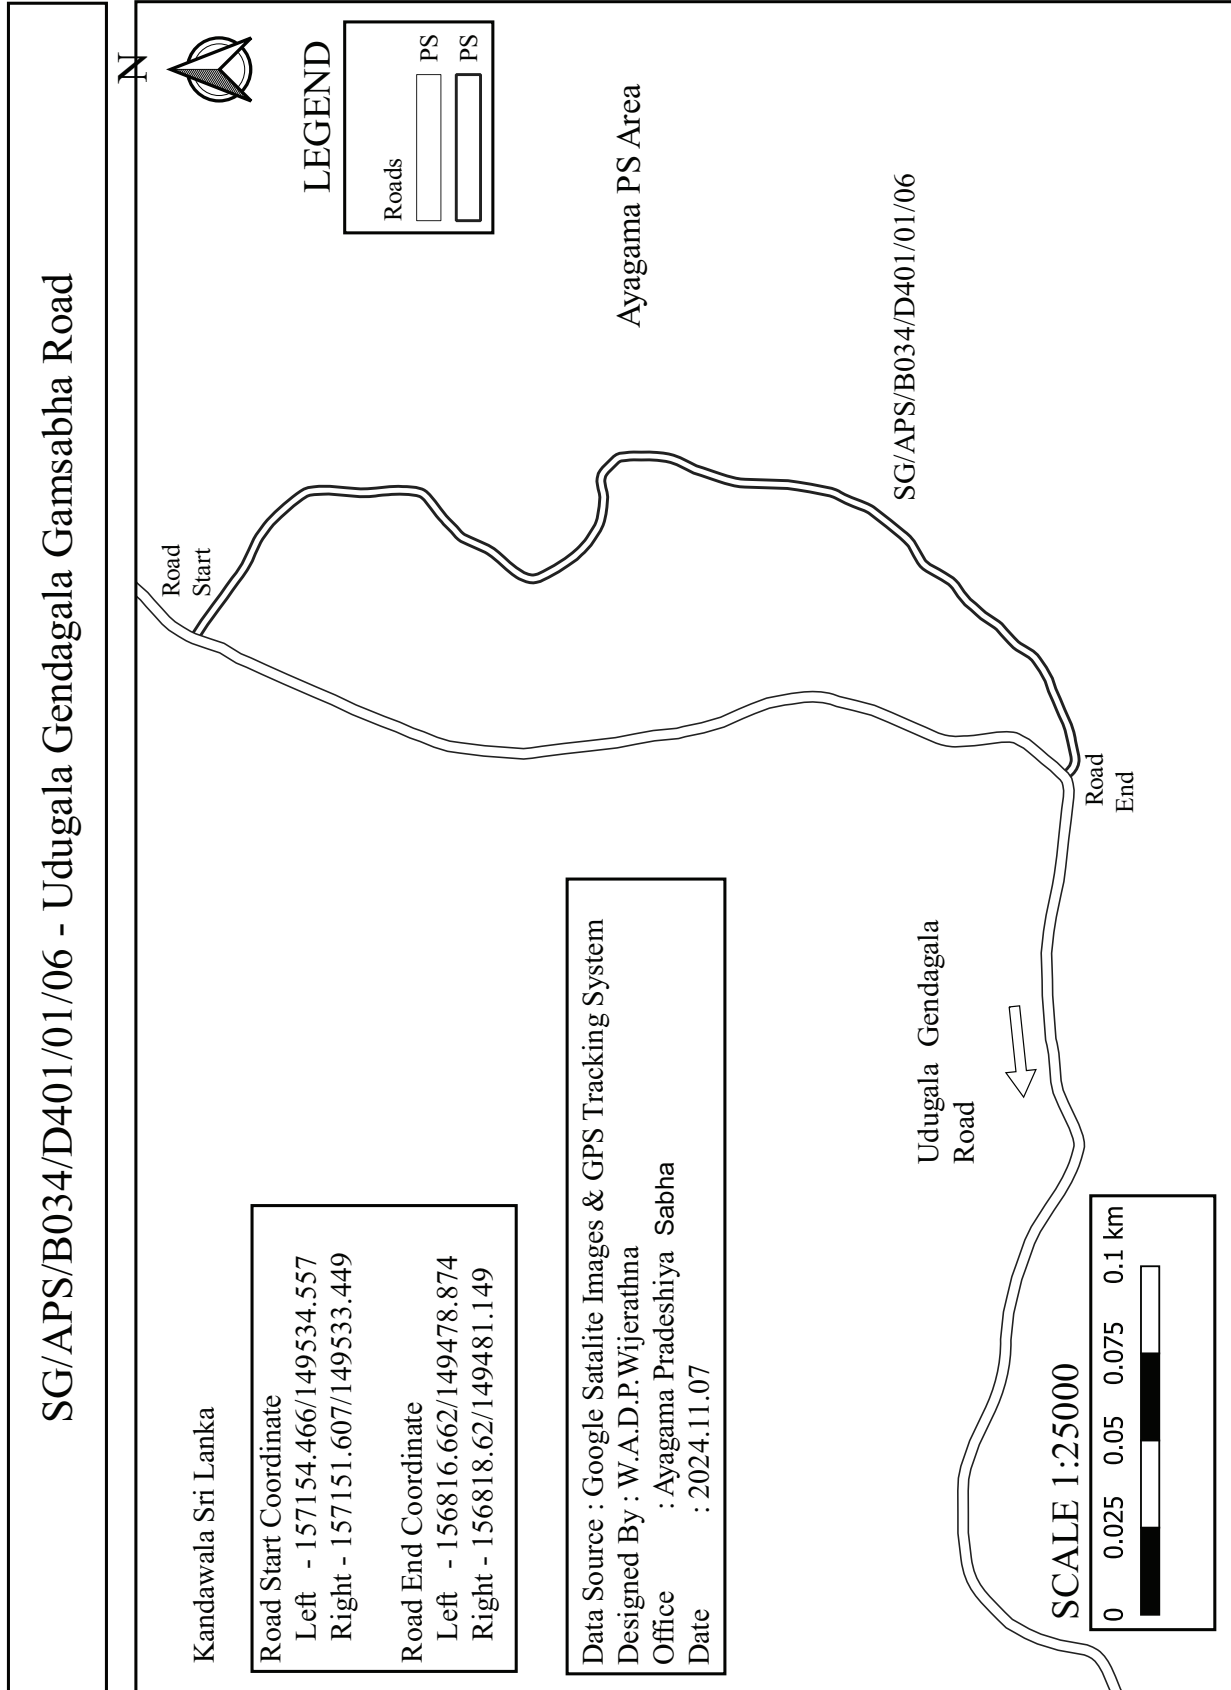

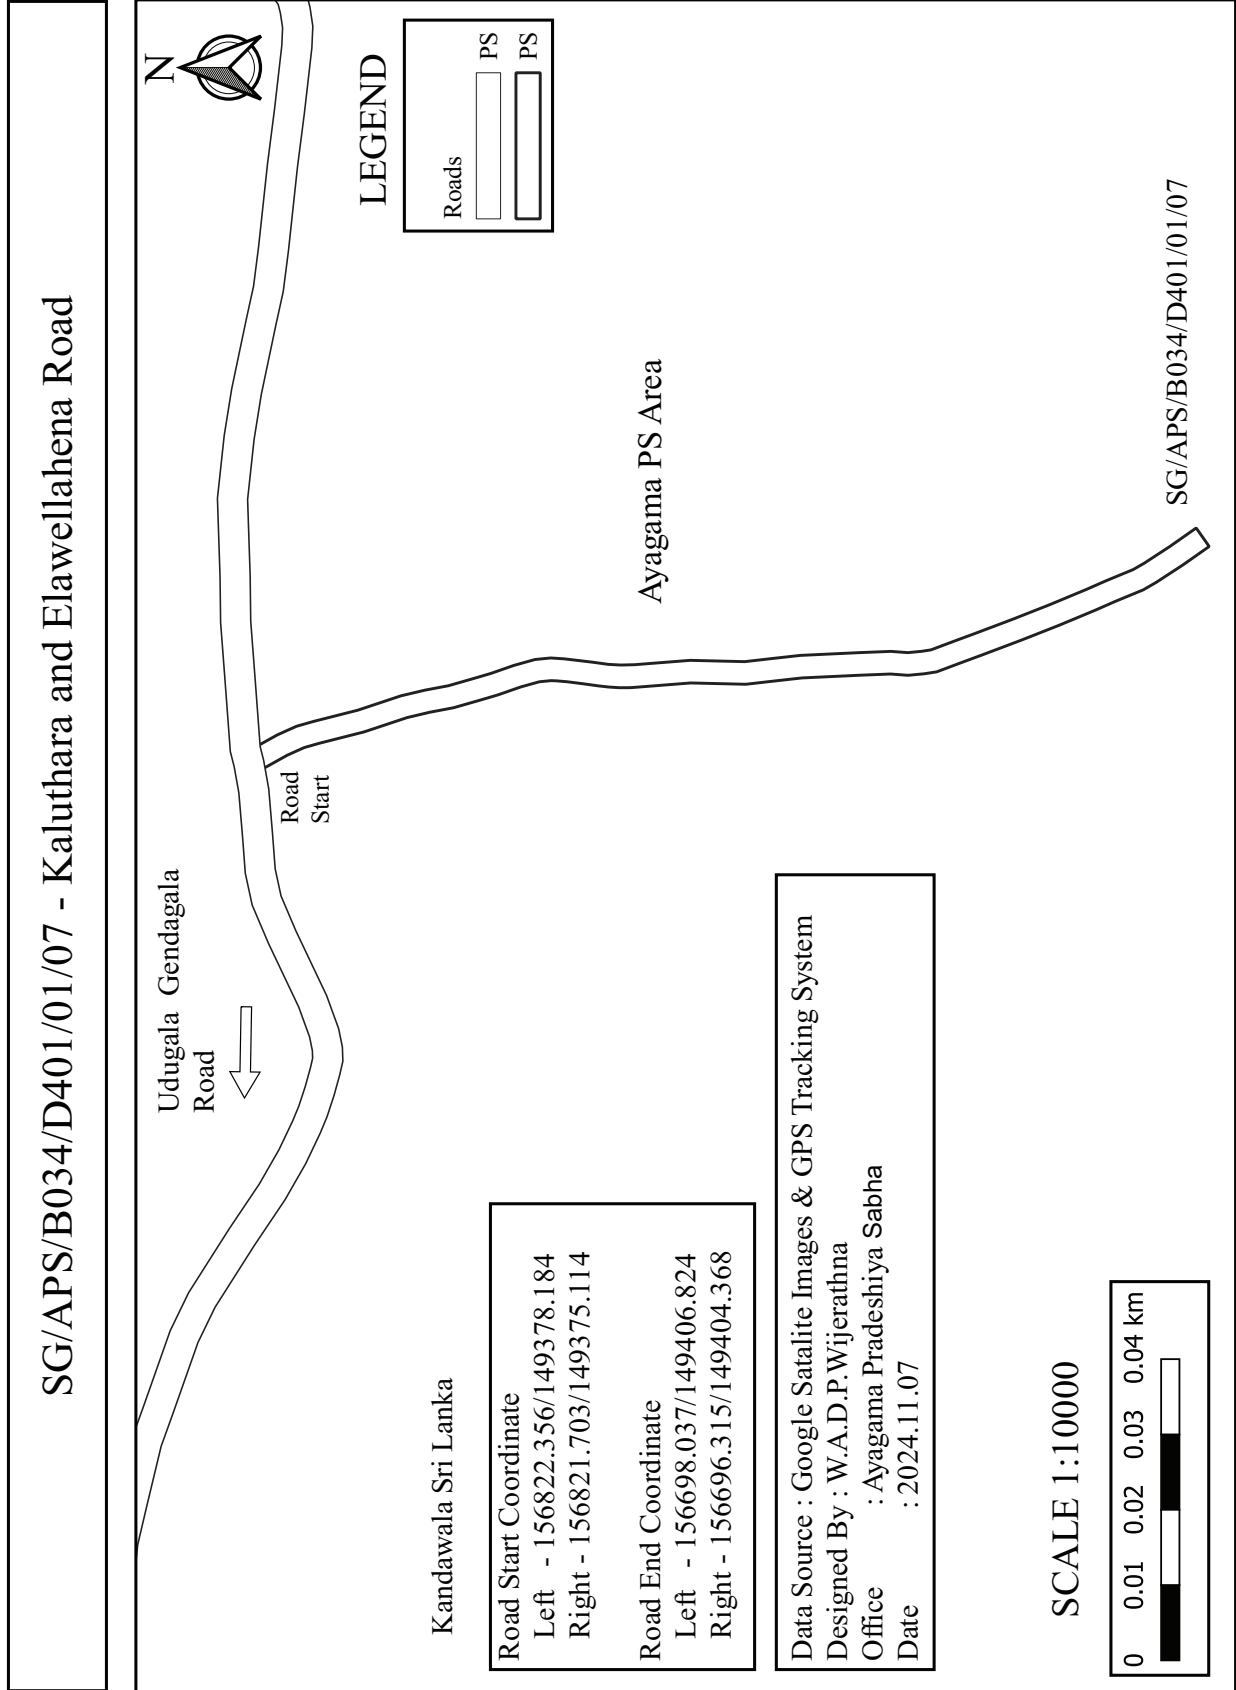



Data Source : Google Satalite Images & GPS Tracking System


Designed By : W.A.D.P.Wijerathna

Office : Ayagama Pradeshiya Sabha

Date : 2024.11.07

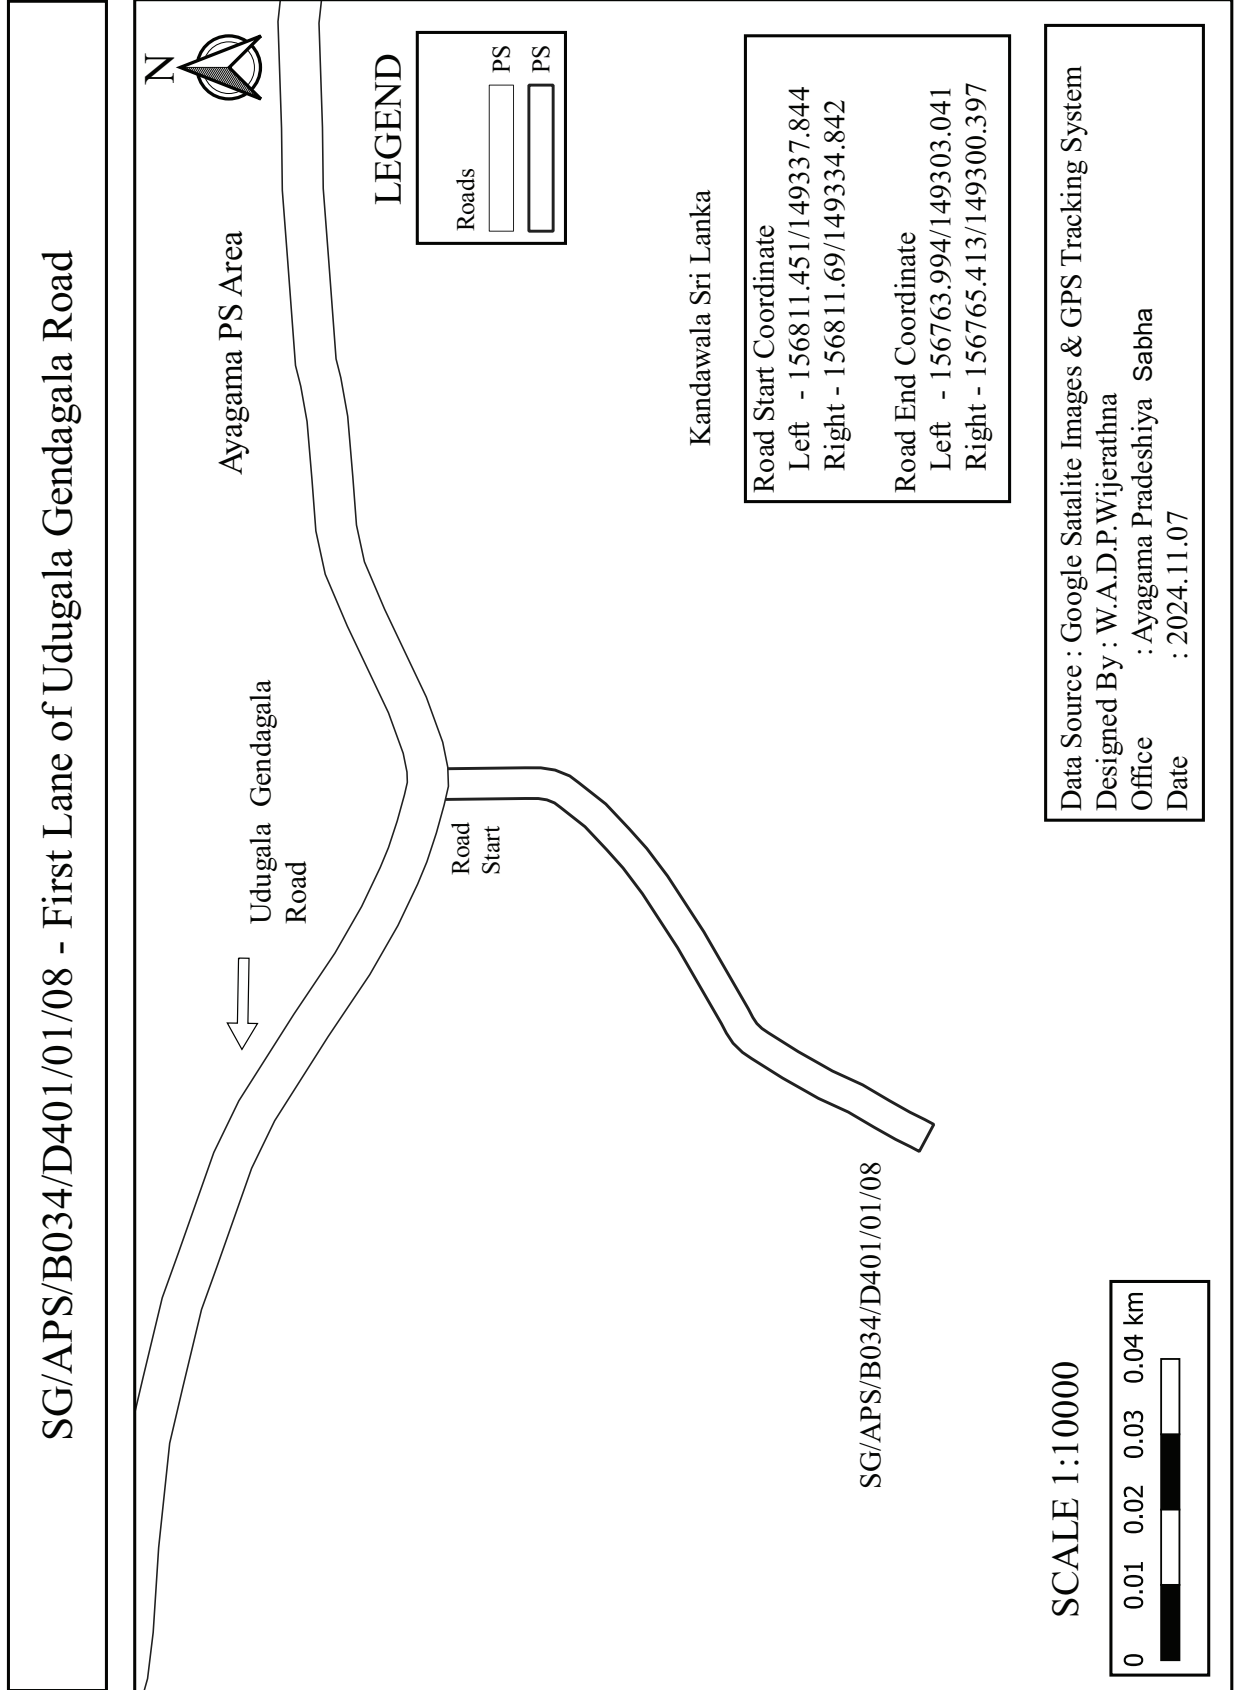

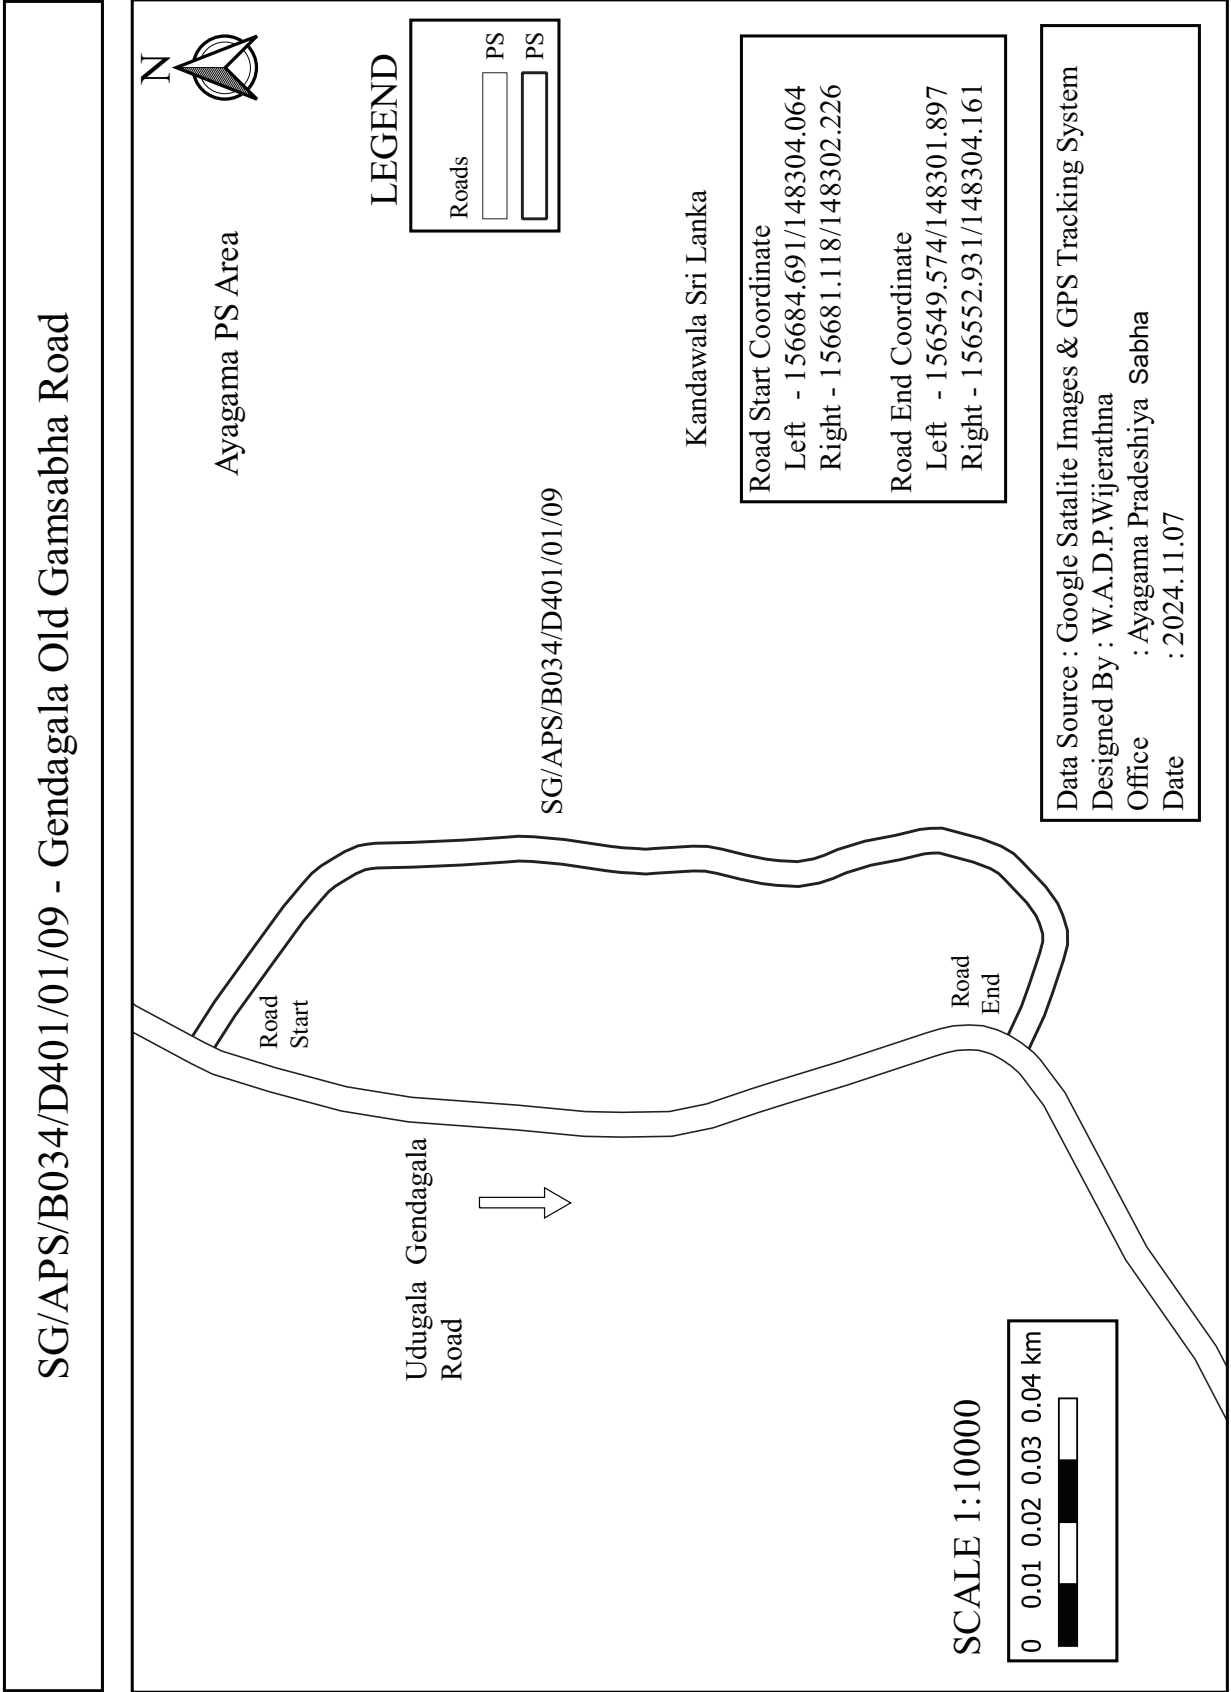

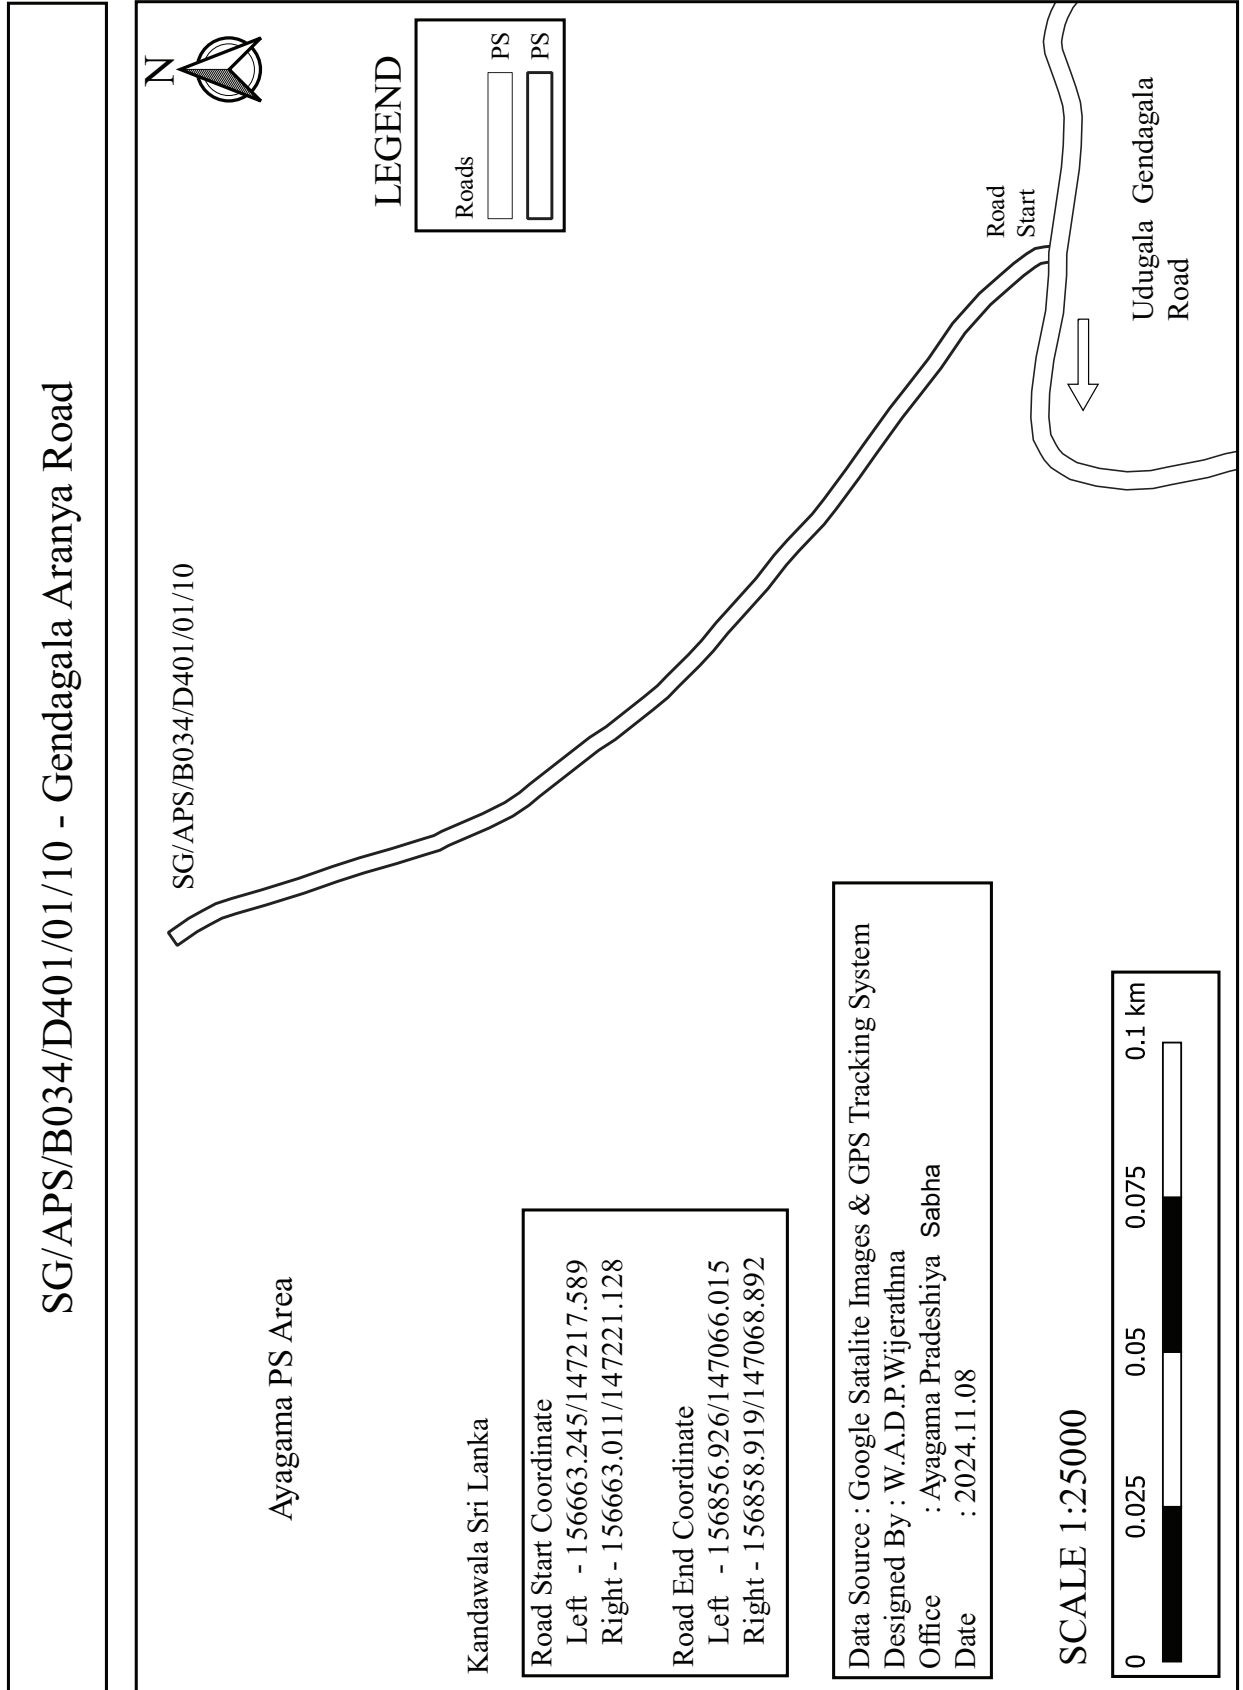

SG/APS/B034/D401/01/11 - Gendagala Hathaliha Waththa Road

Data Source : Google Satalite Images & GPS Tracking System
Designed By : W.A.D.P.Wijerathna
Office : Ayagama Pradeshiya Sabha
Date : 2024.11.08

Ayagama PS Area

LEGEND

Roads

PS

PS

Road Start

SG/APS/B034/D401/01/11

Kandawala Sri Lanka

Road Start Coordinate

Left - 156531.734/147168.814

Right - 156534.705/147170.276


Road End Coordinate


Left - 156588.076/146855.55


Right - 156590.973/146856.33


SCALE 1:25000


0	0.025	0.05	0.075	0.1 km
---	-------	------	-------	--------

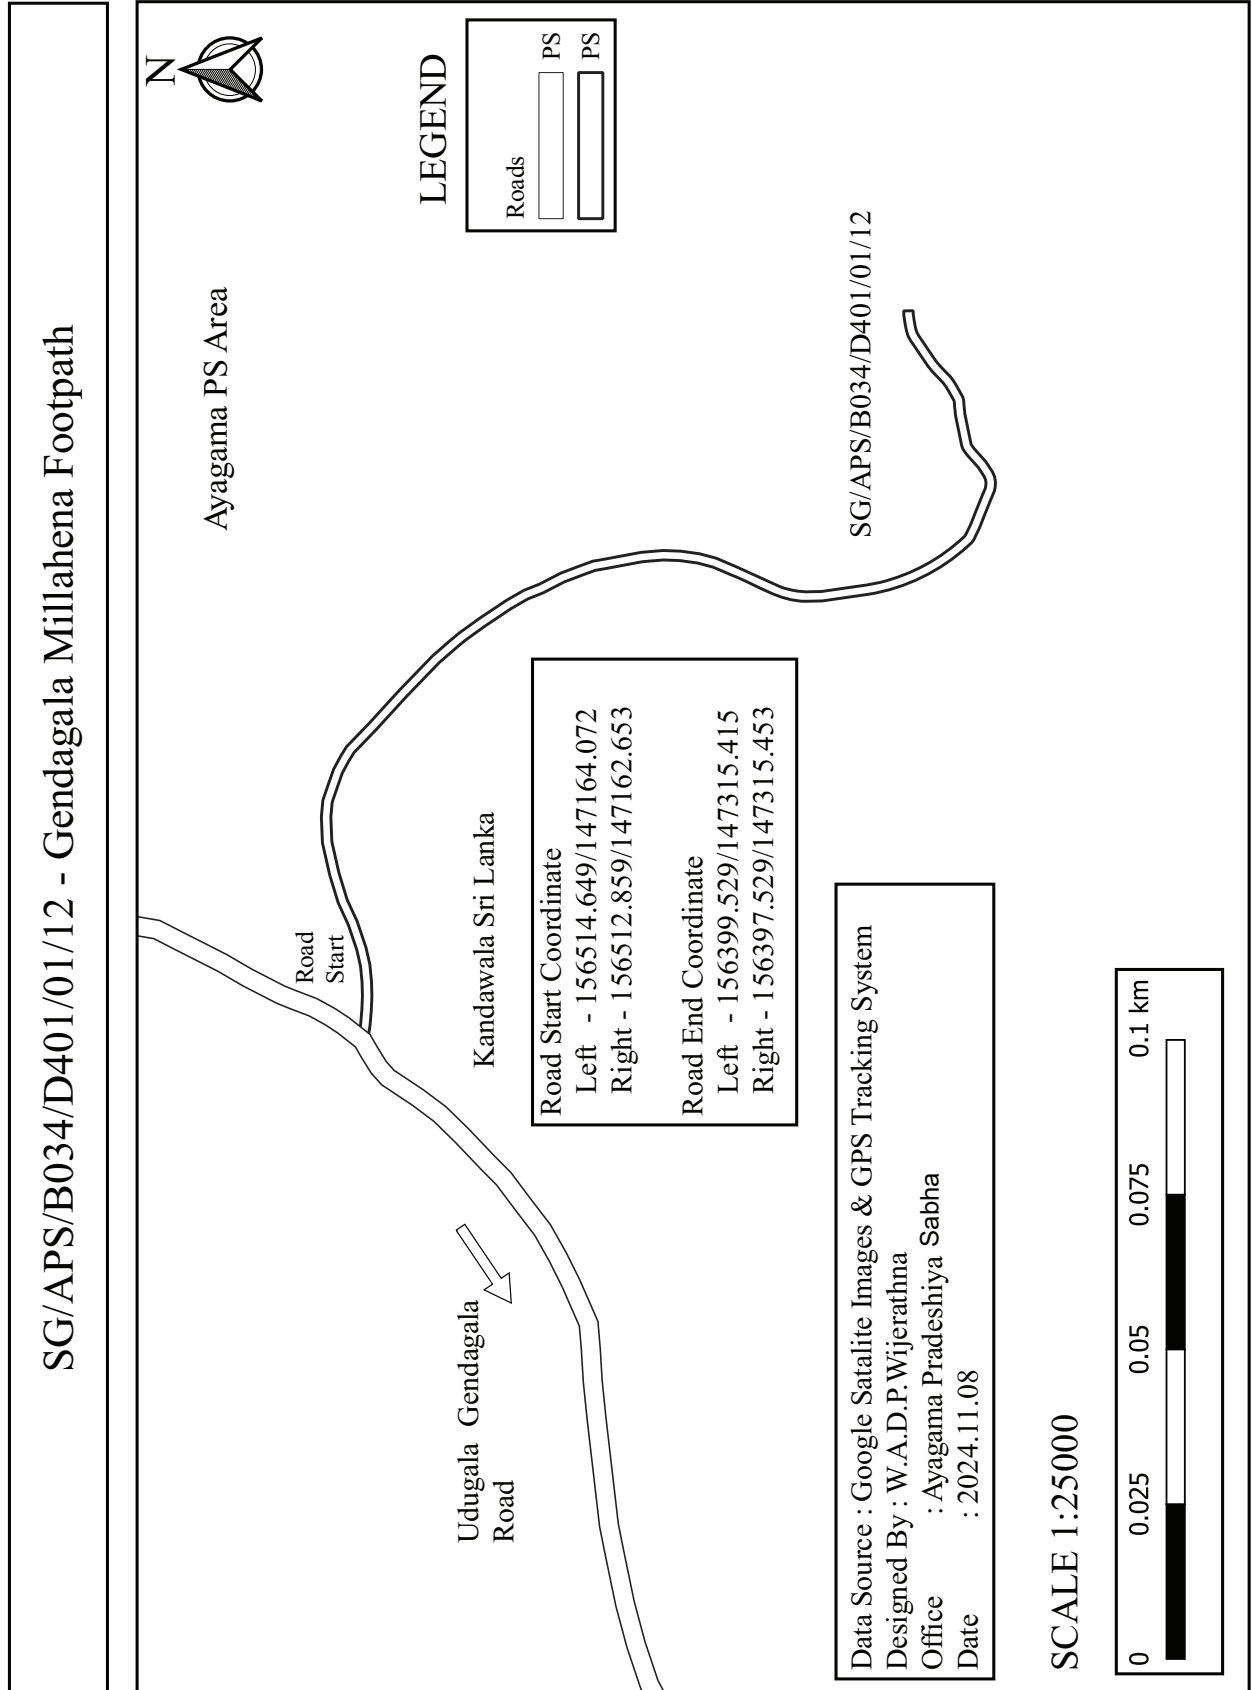


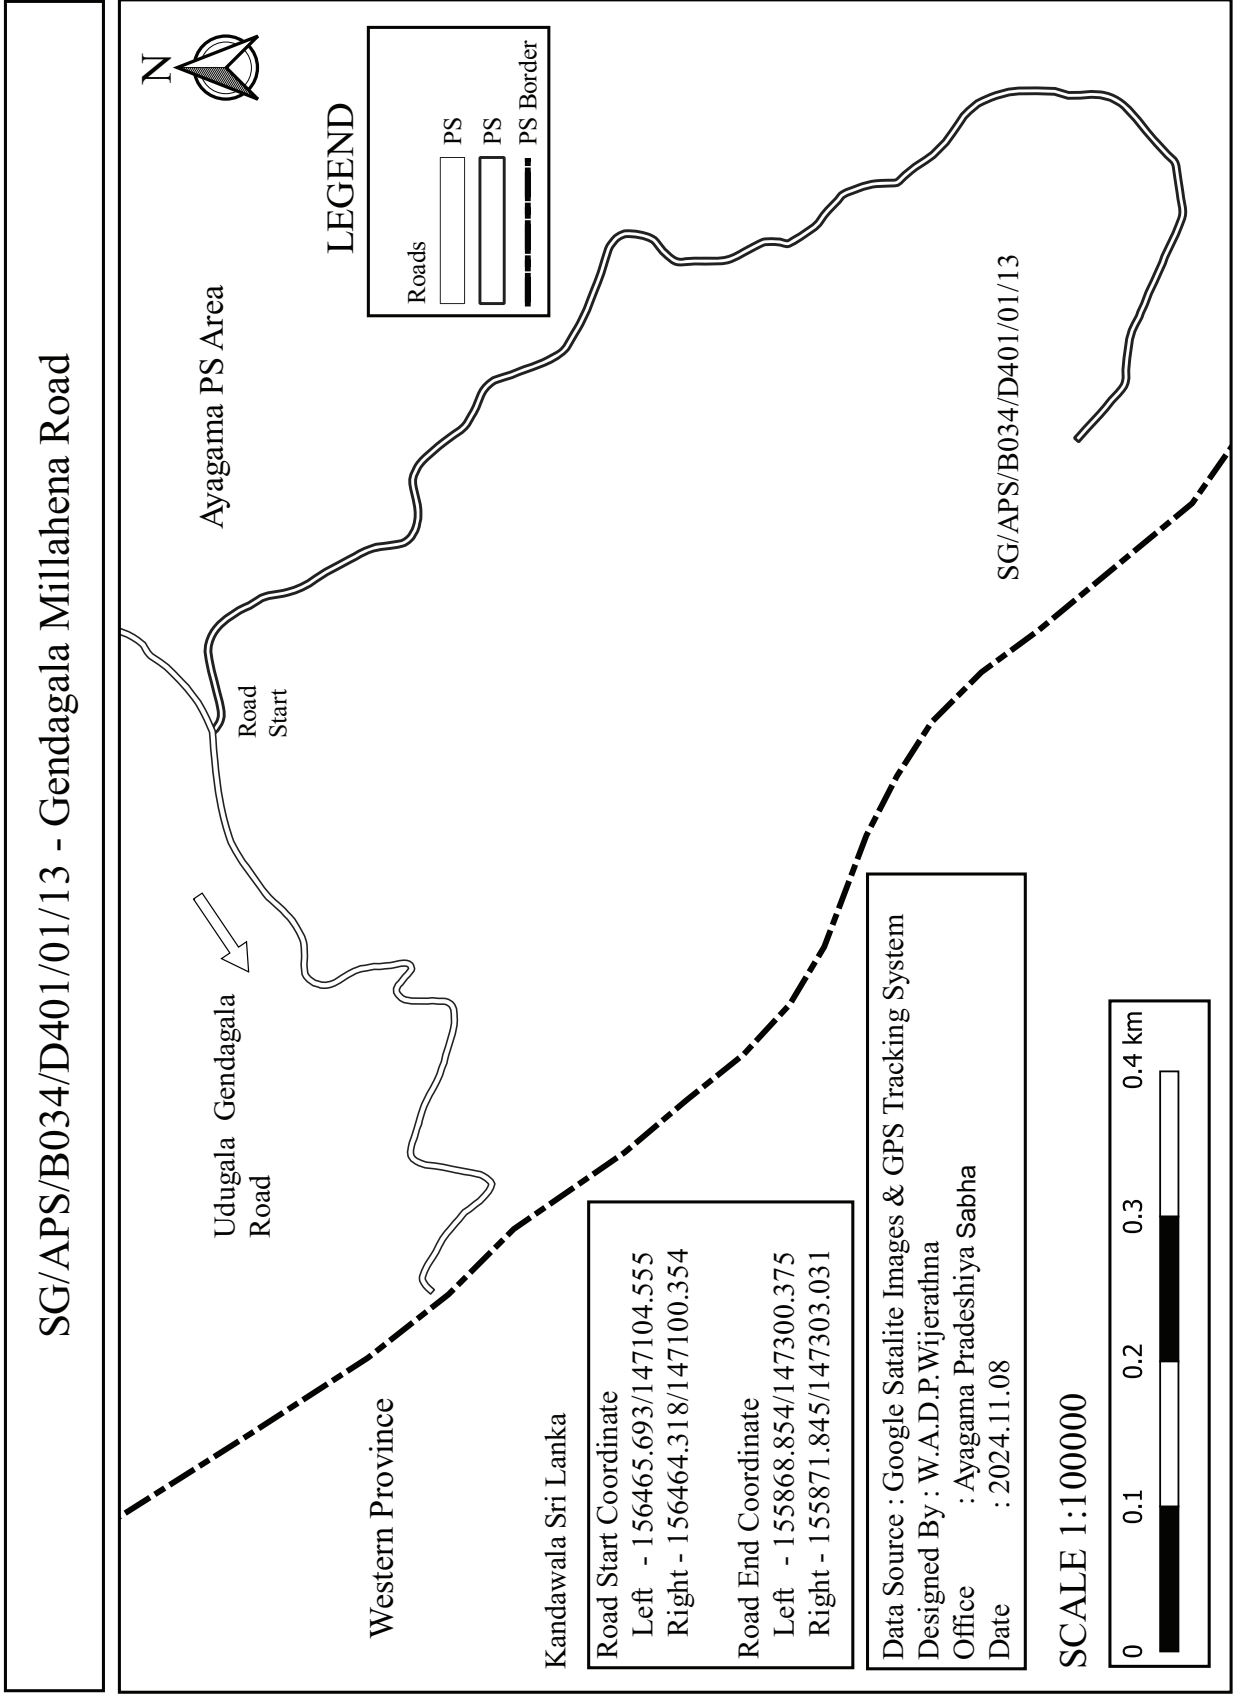


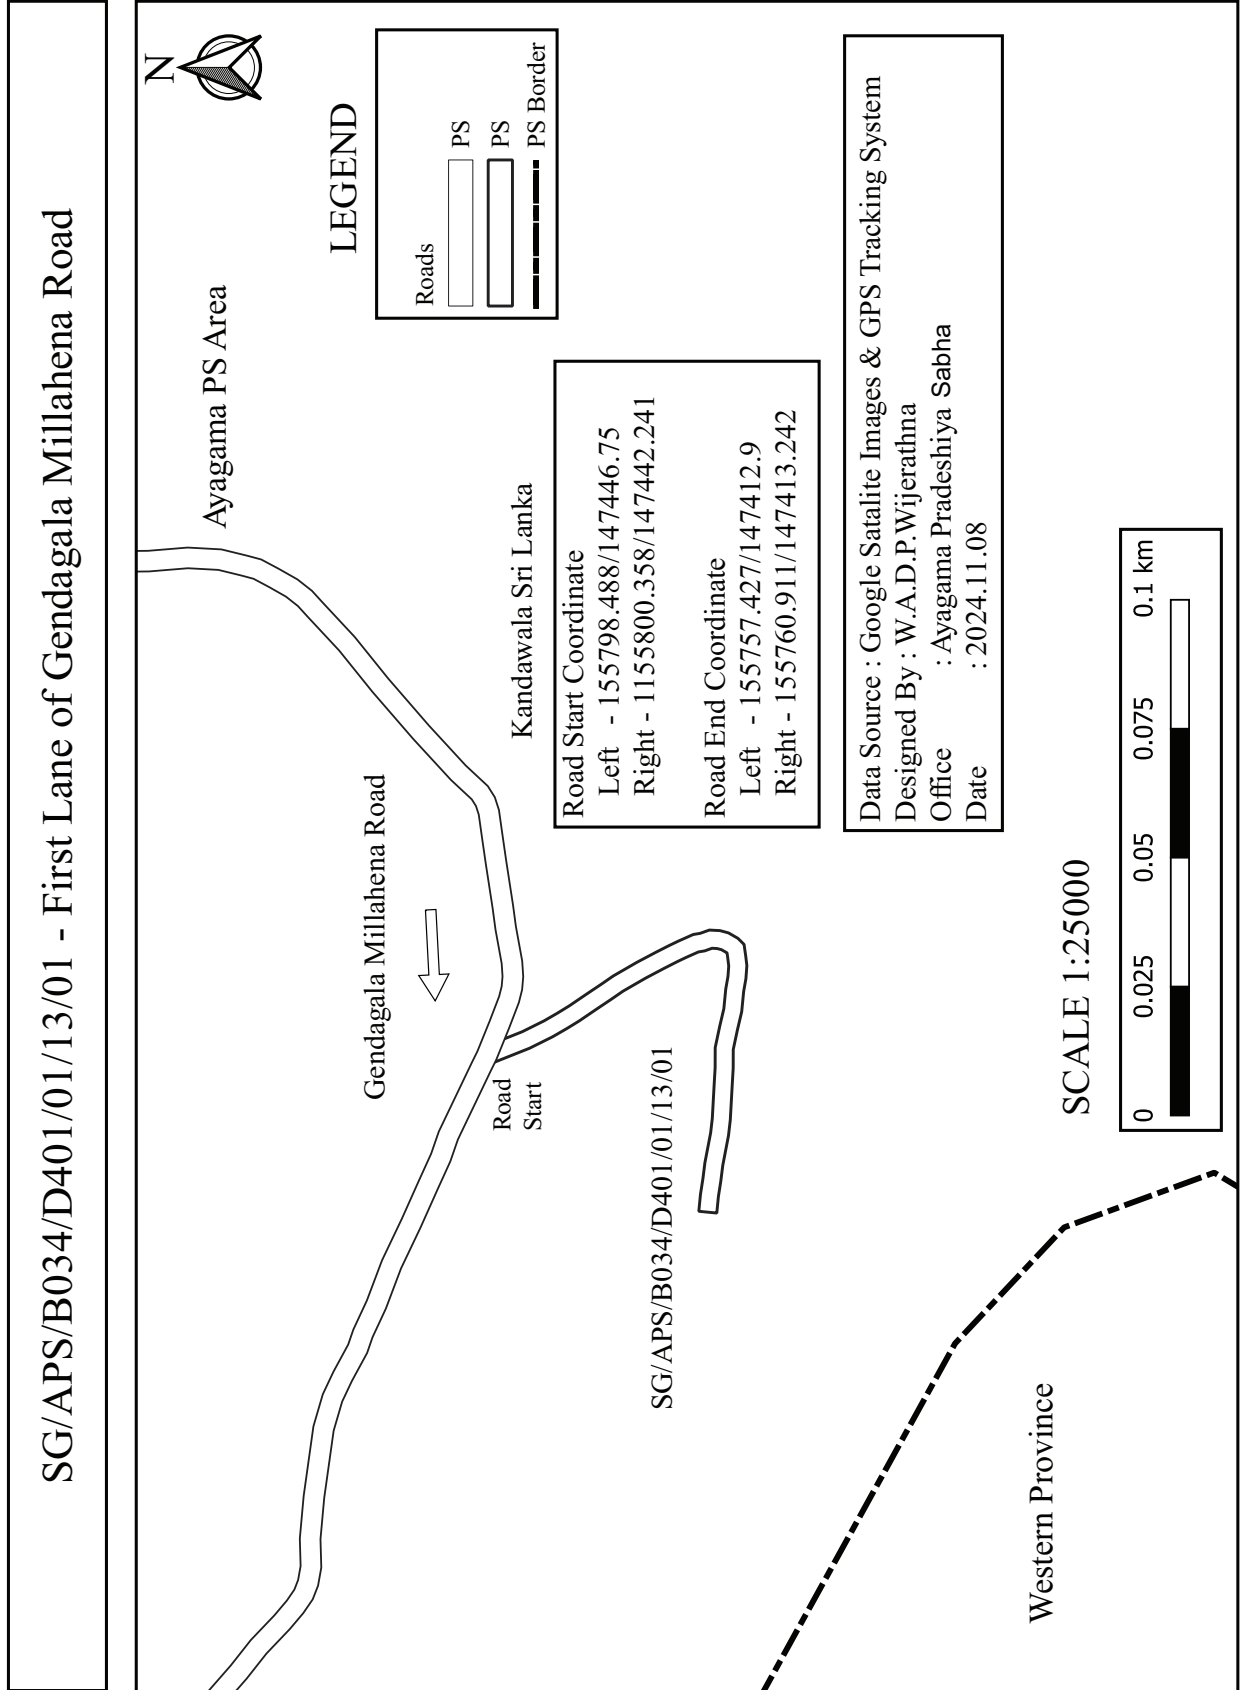

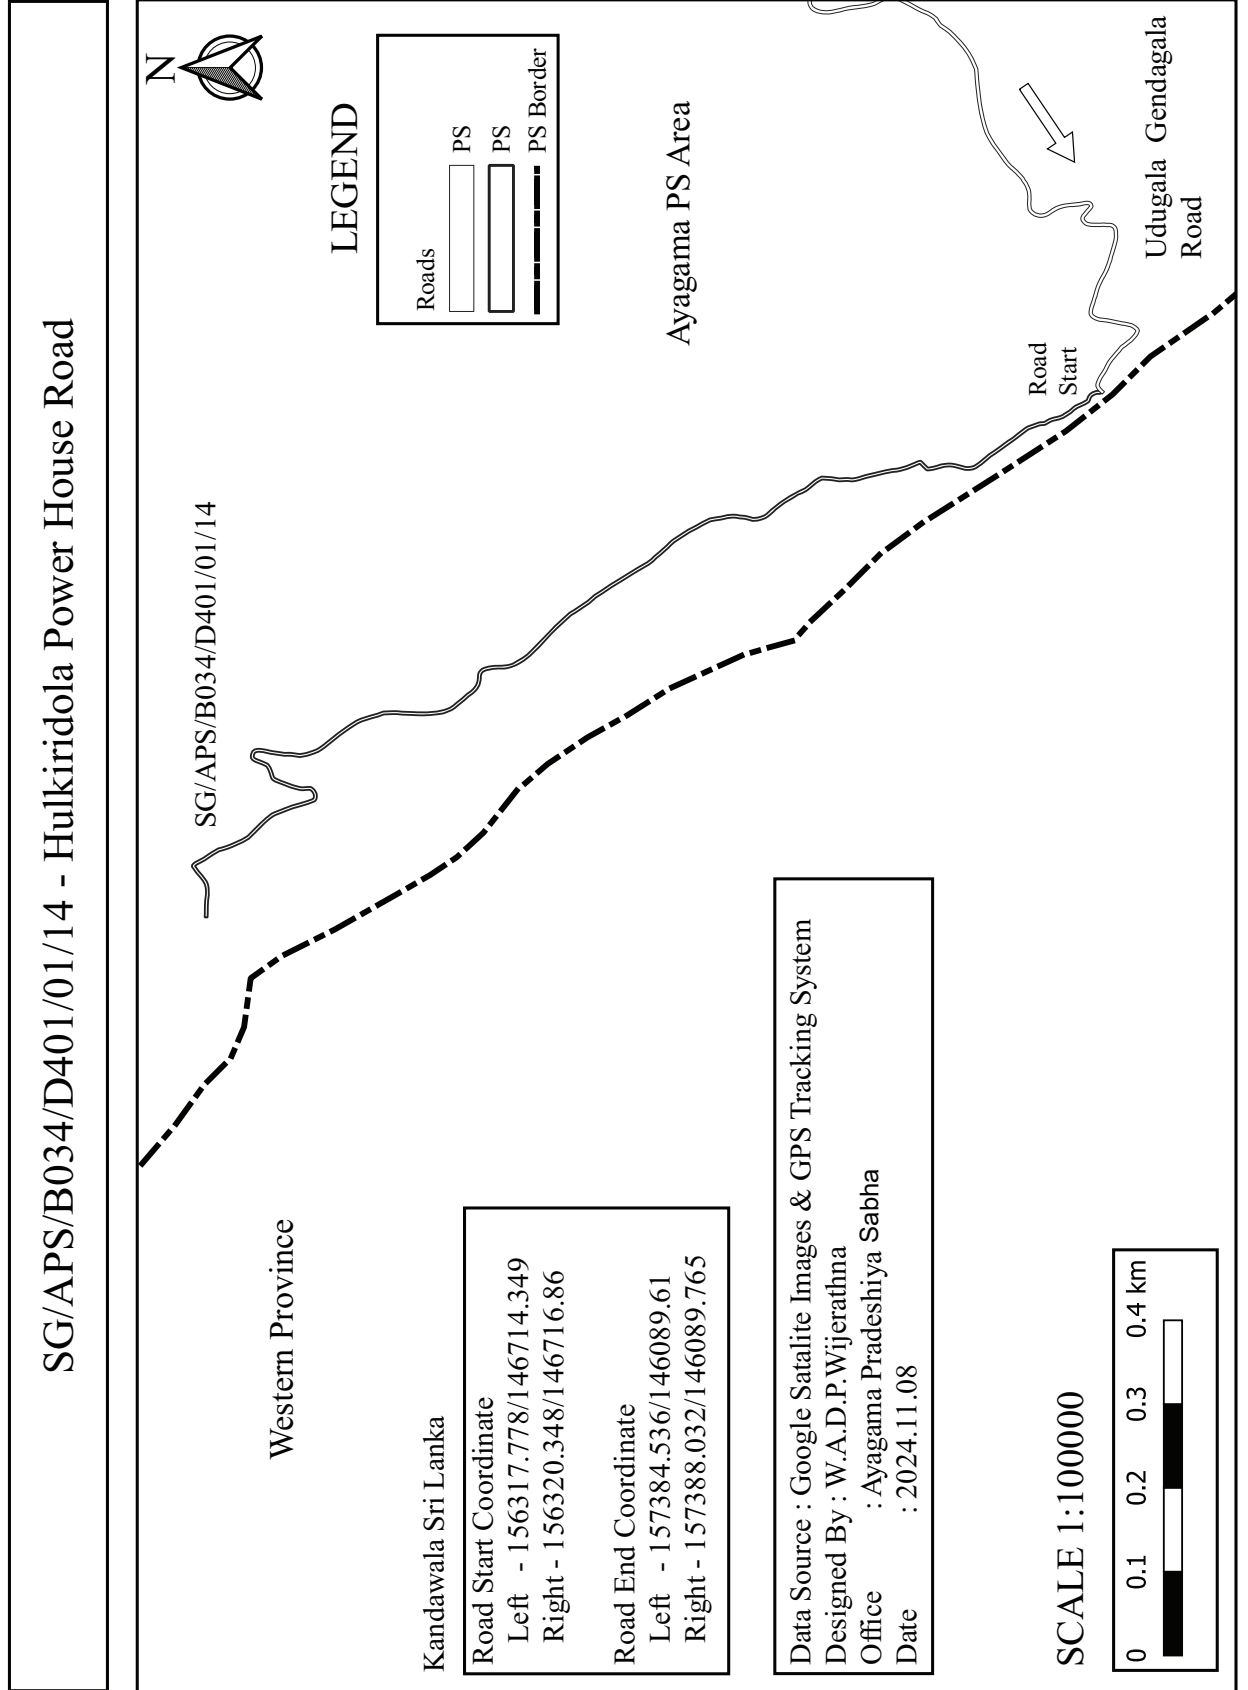


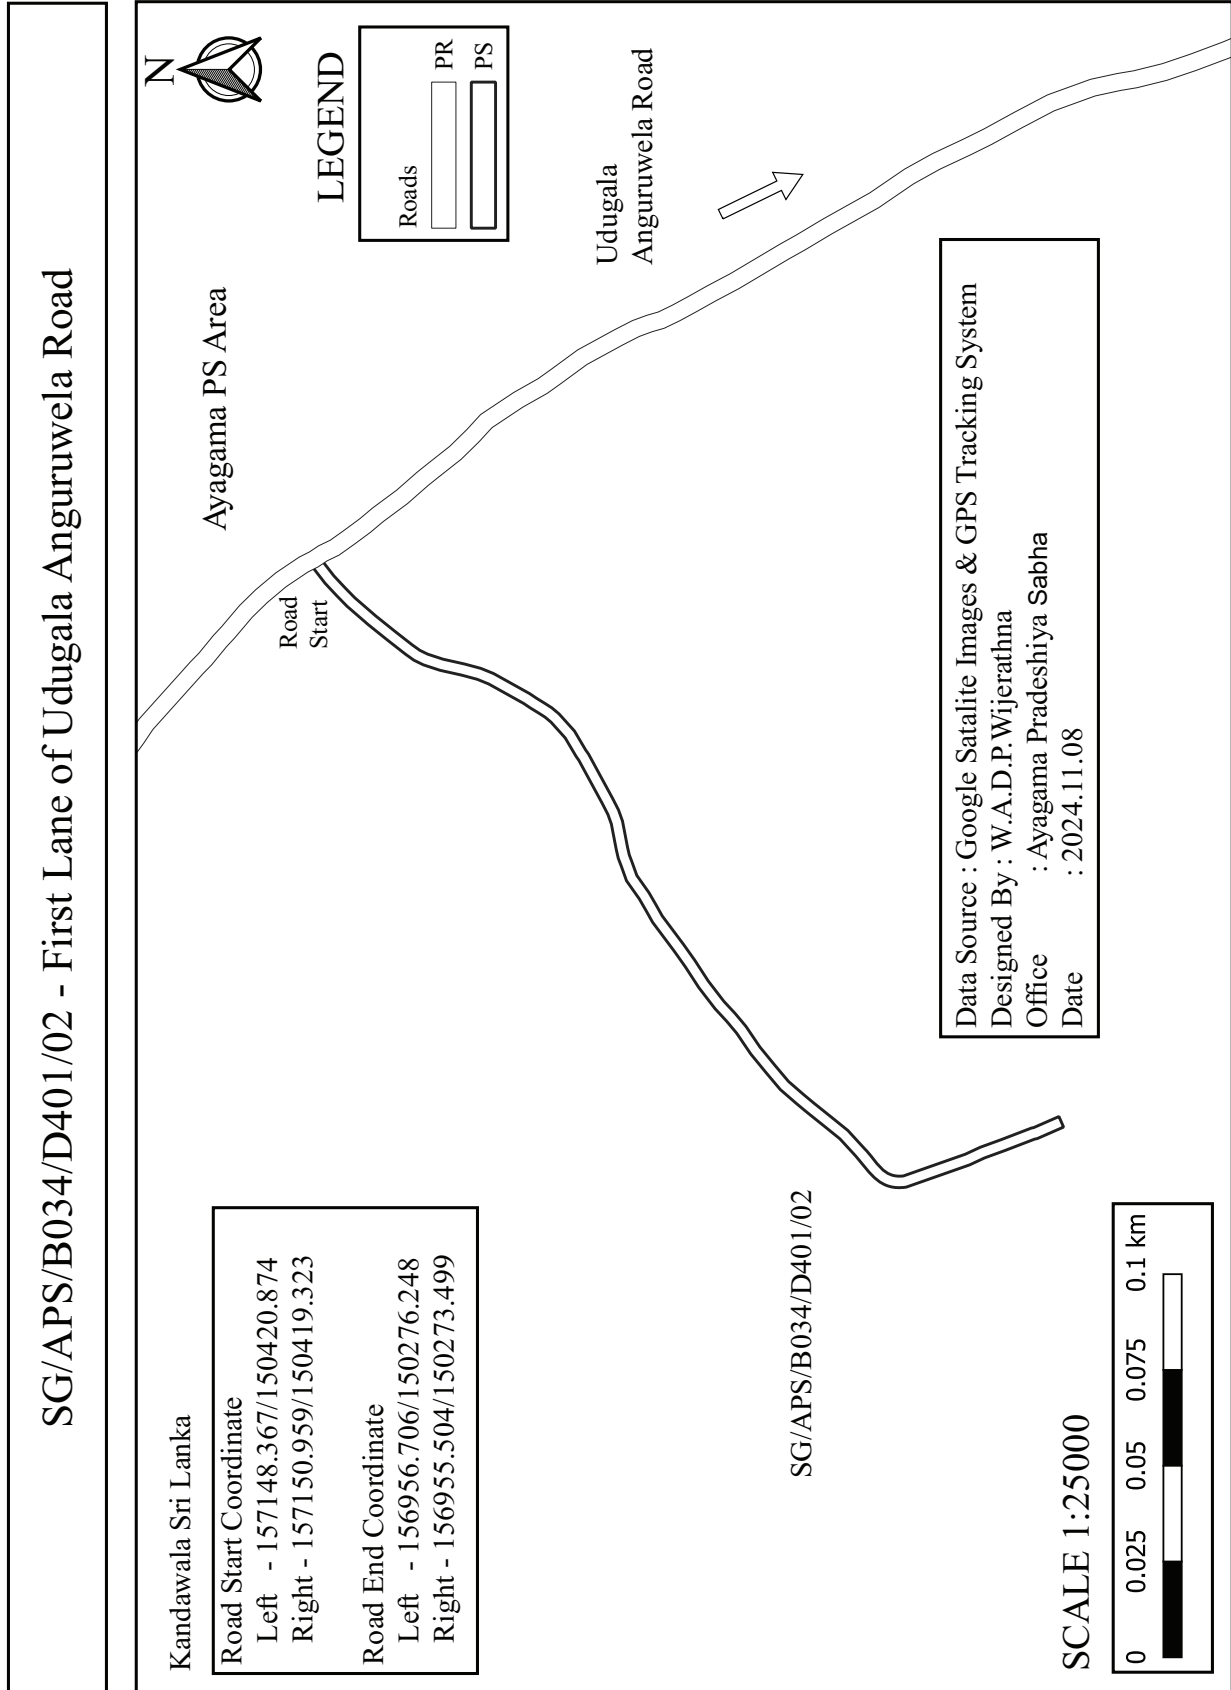


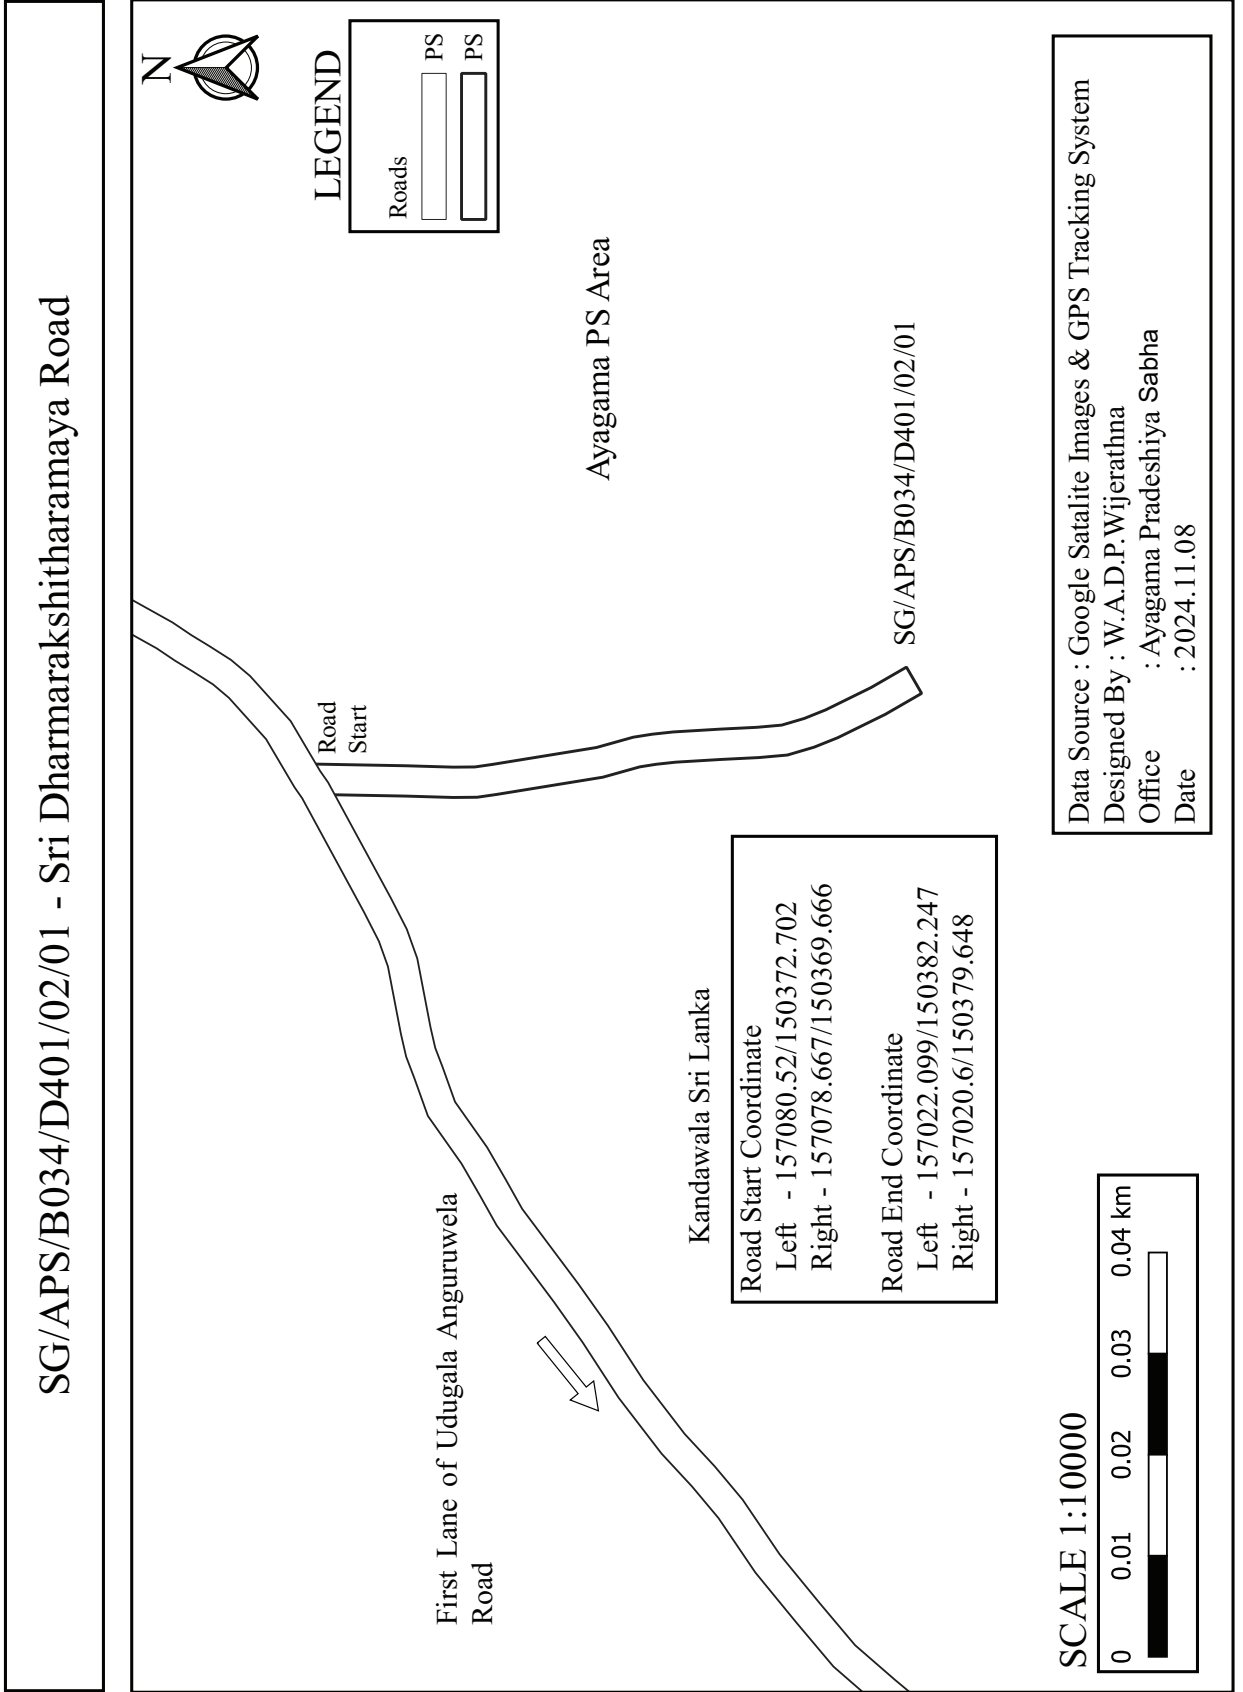


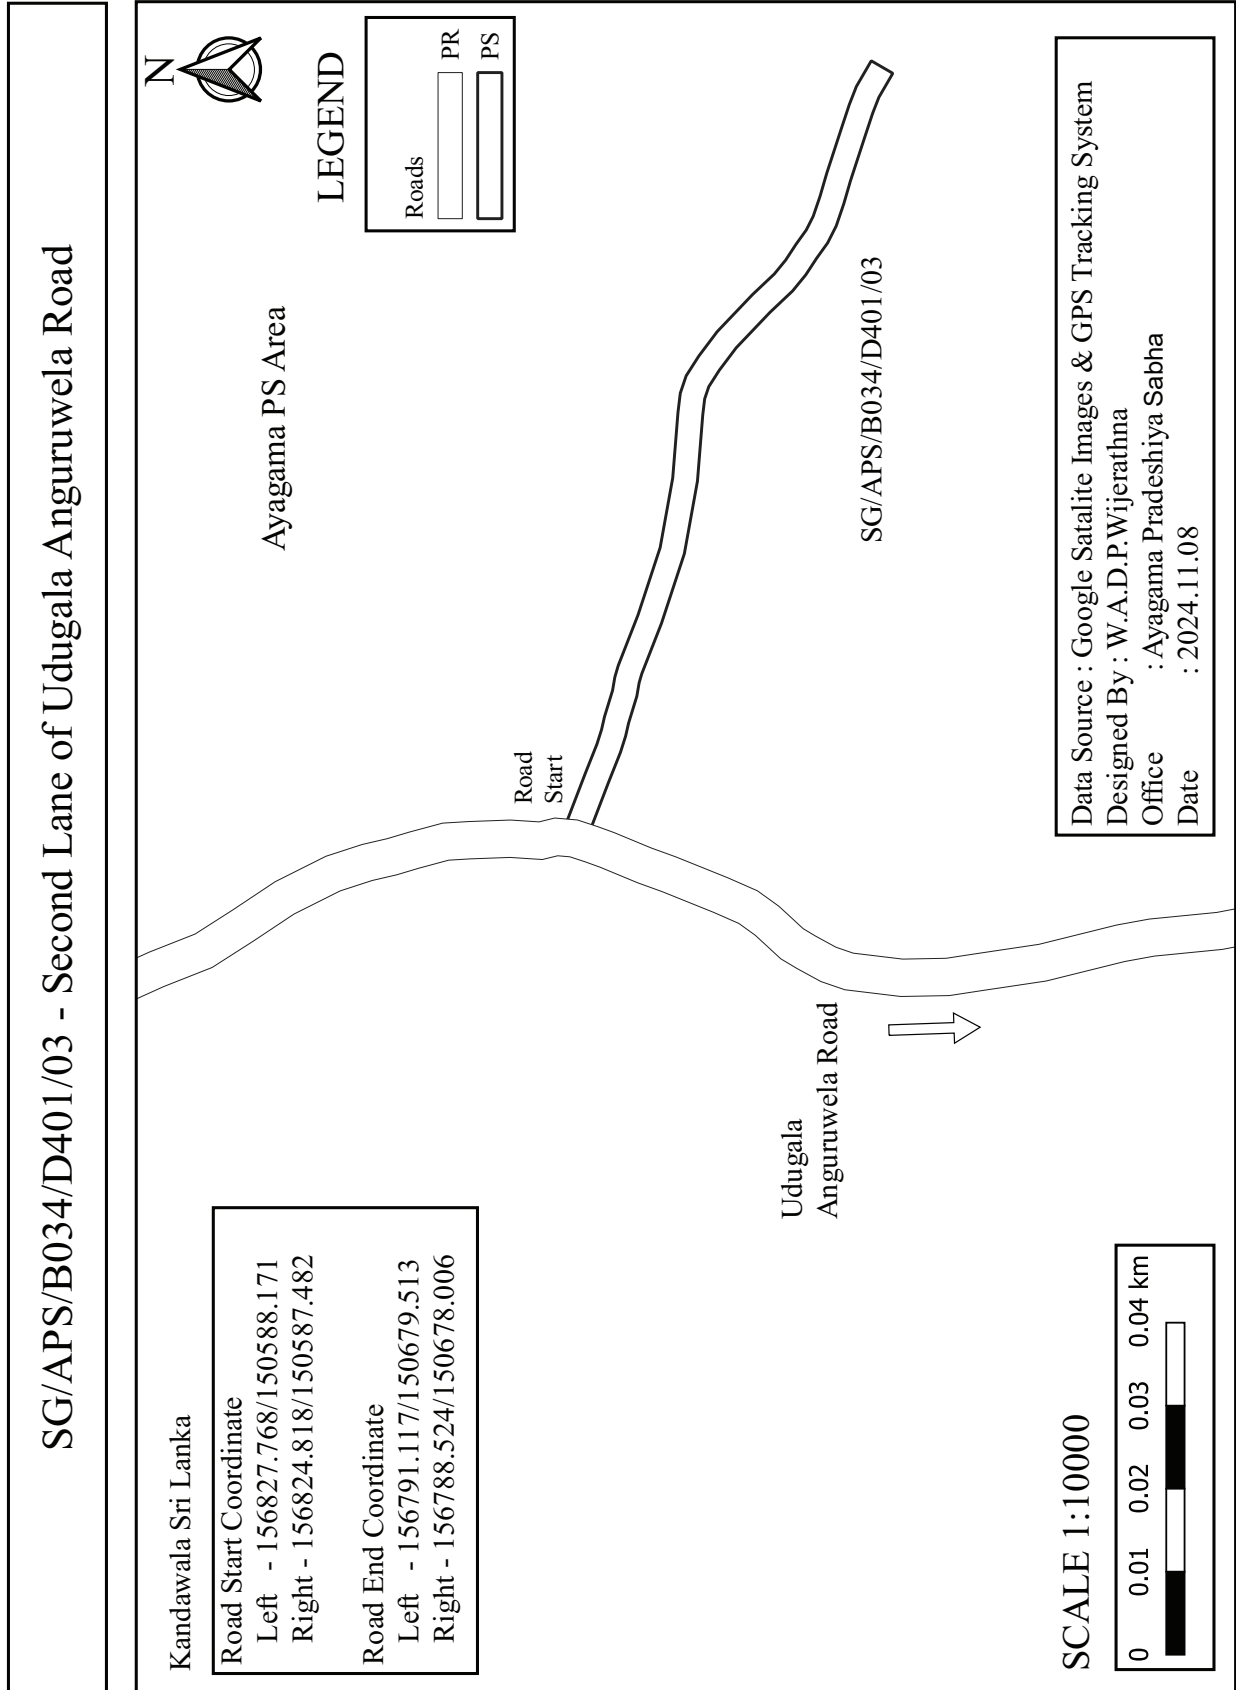


SG/APS/B034/D401/04 - First Road of Anguruwela Finehill Waththa

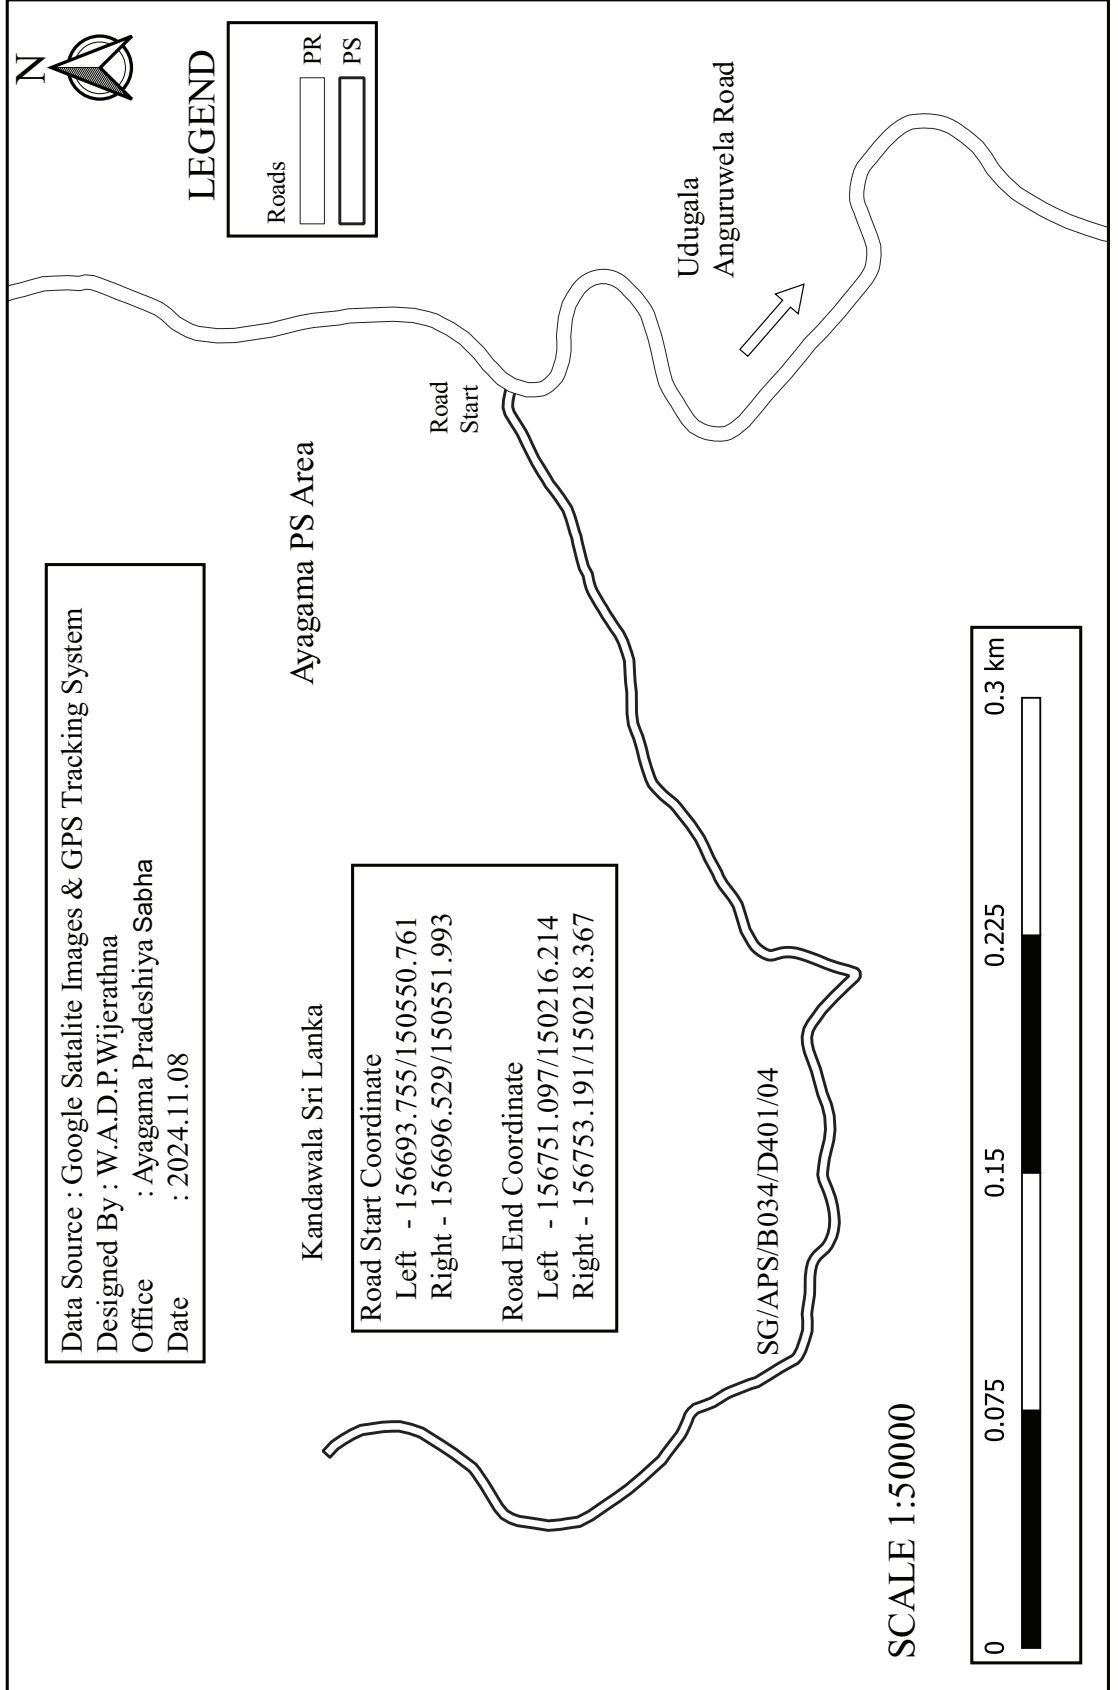


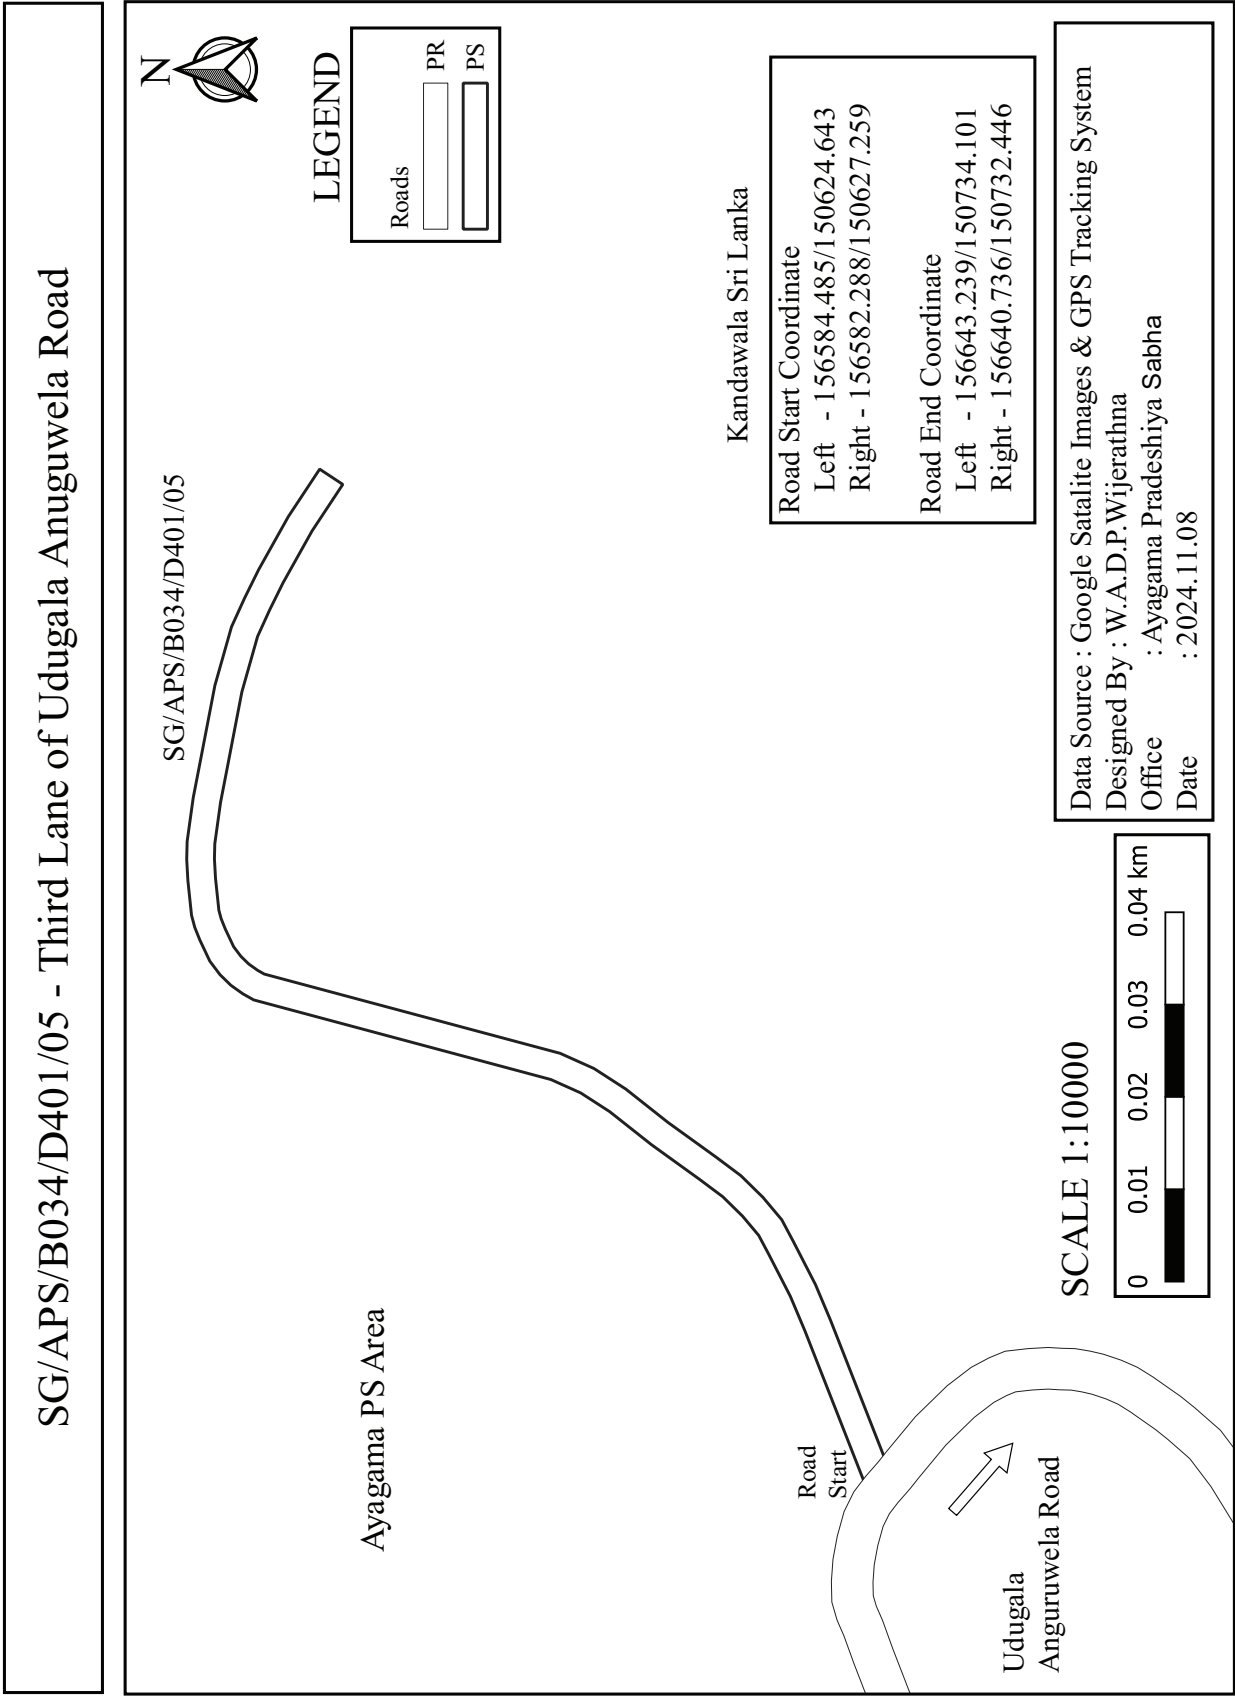


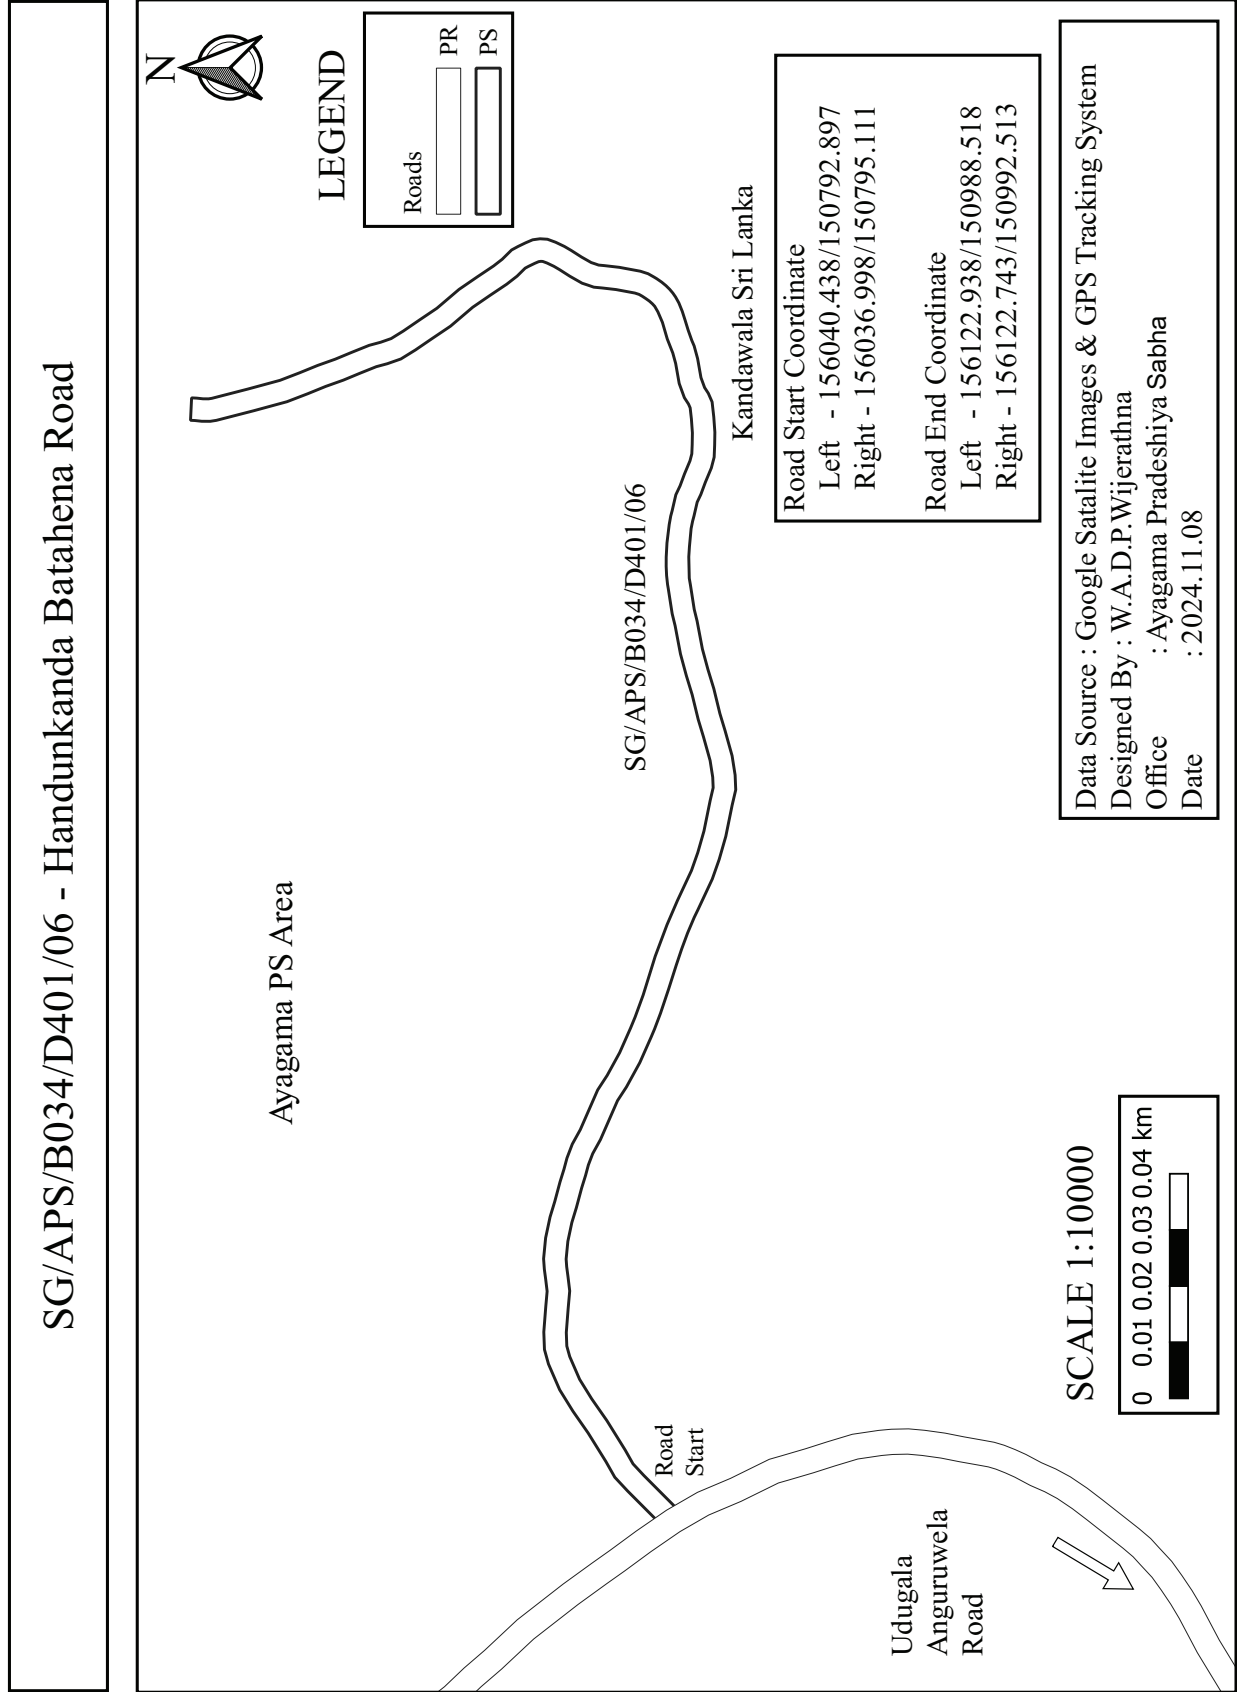


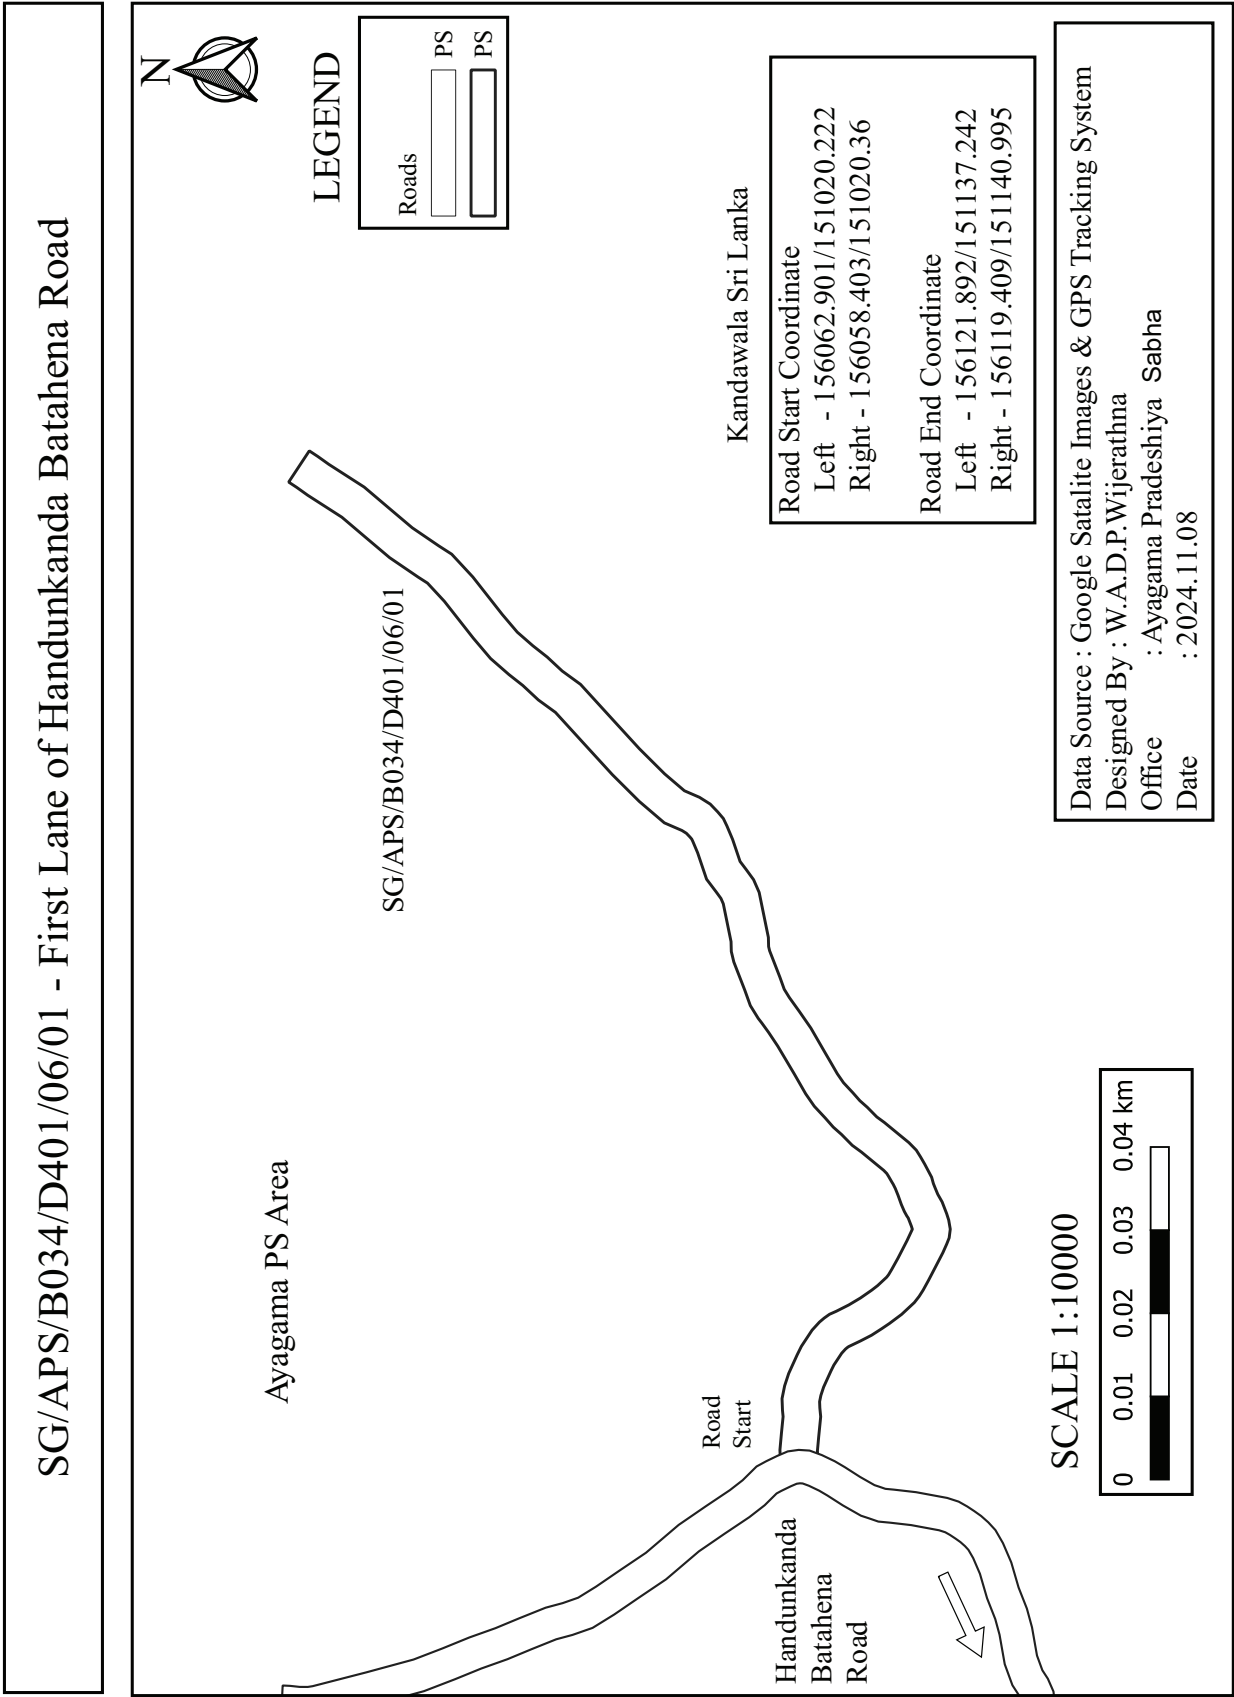


SG/APS/B034/D401/07 - Handunkanda School Road

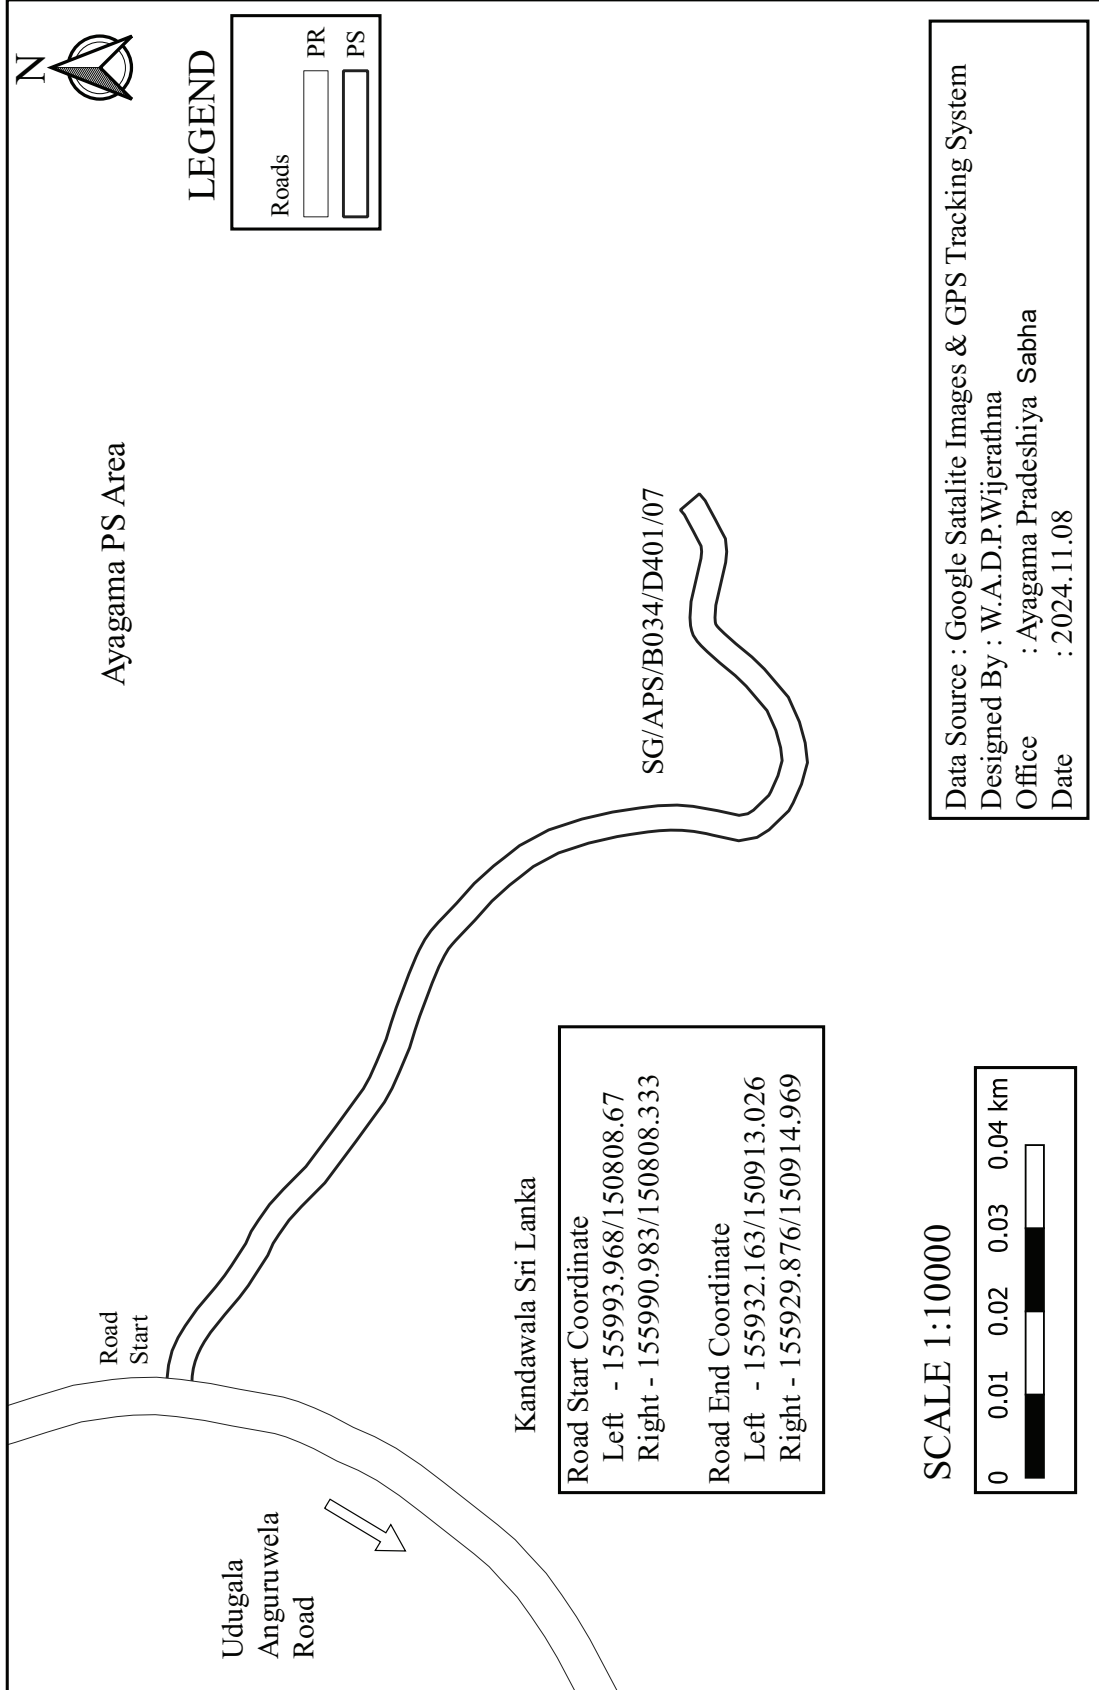


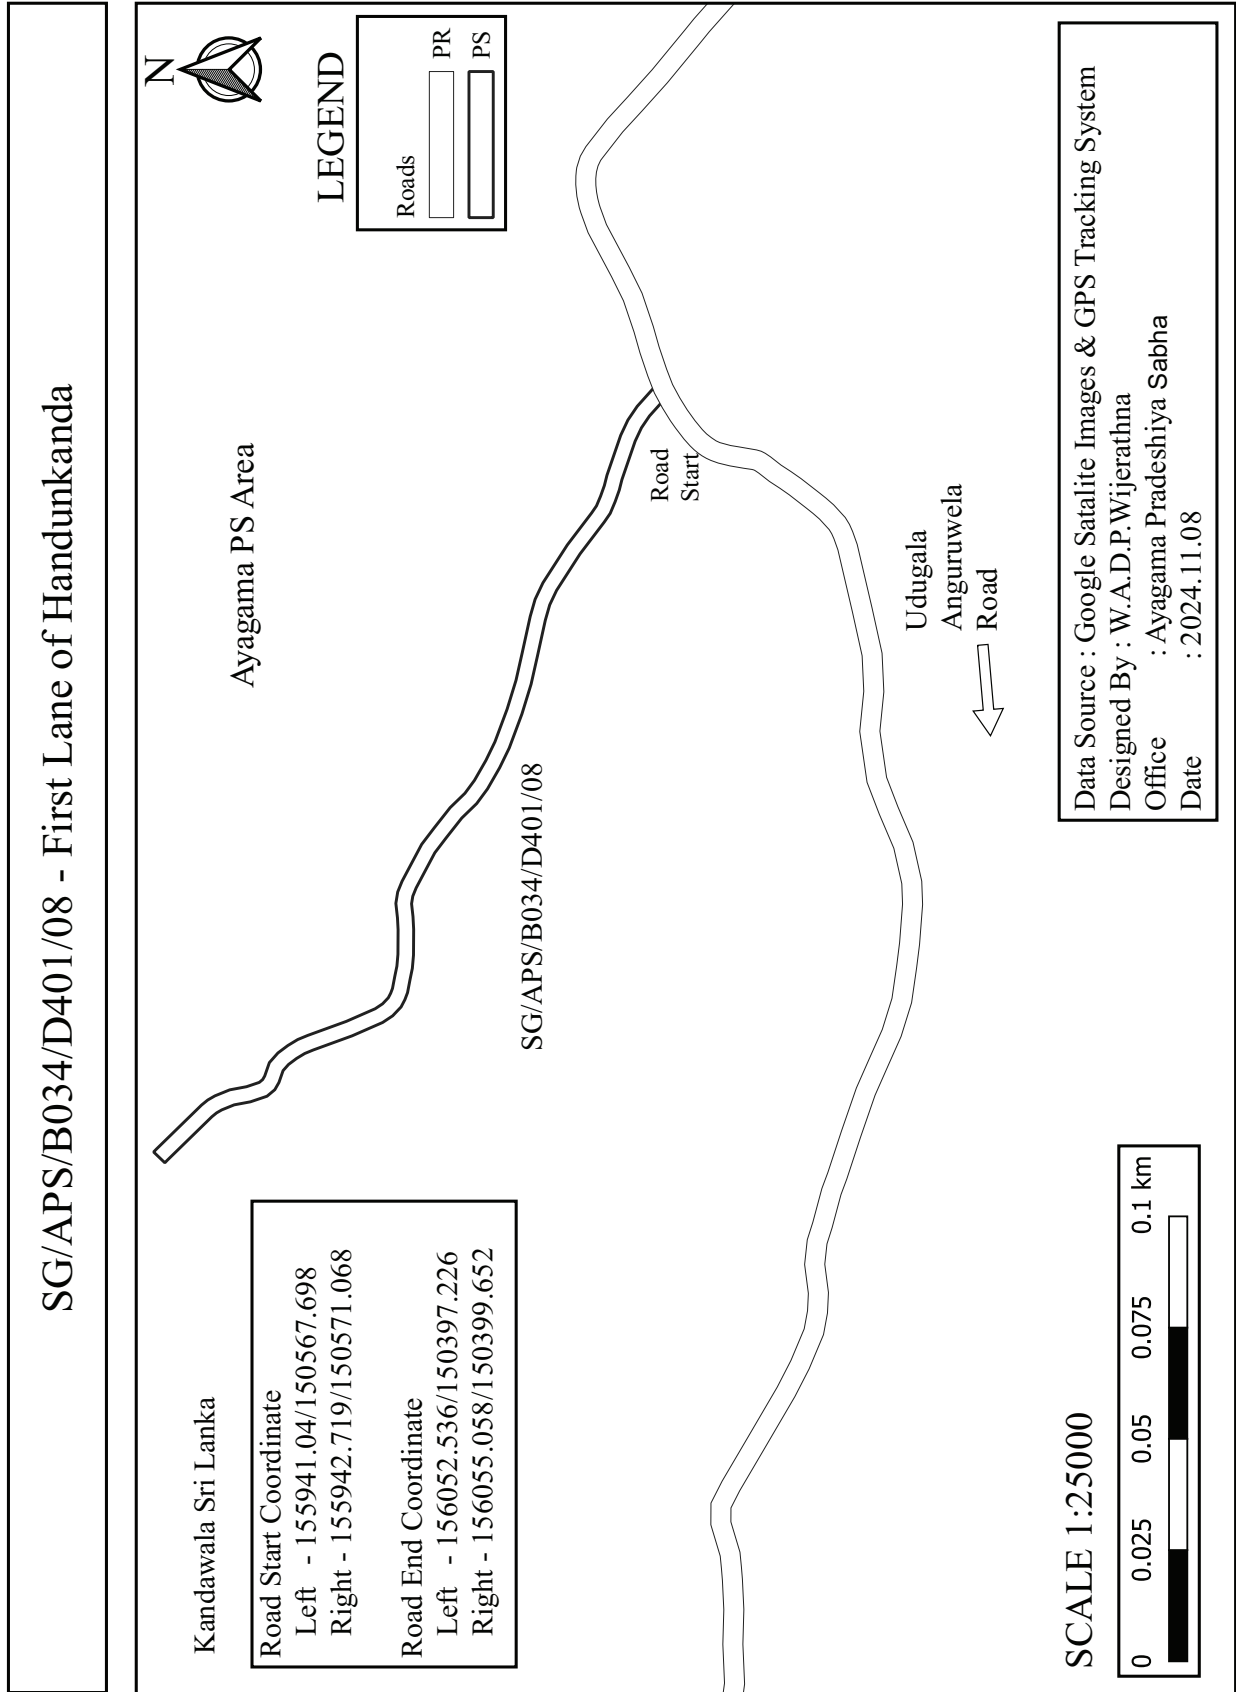

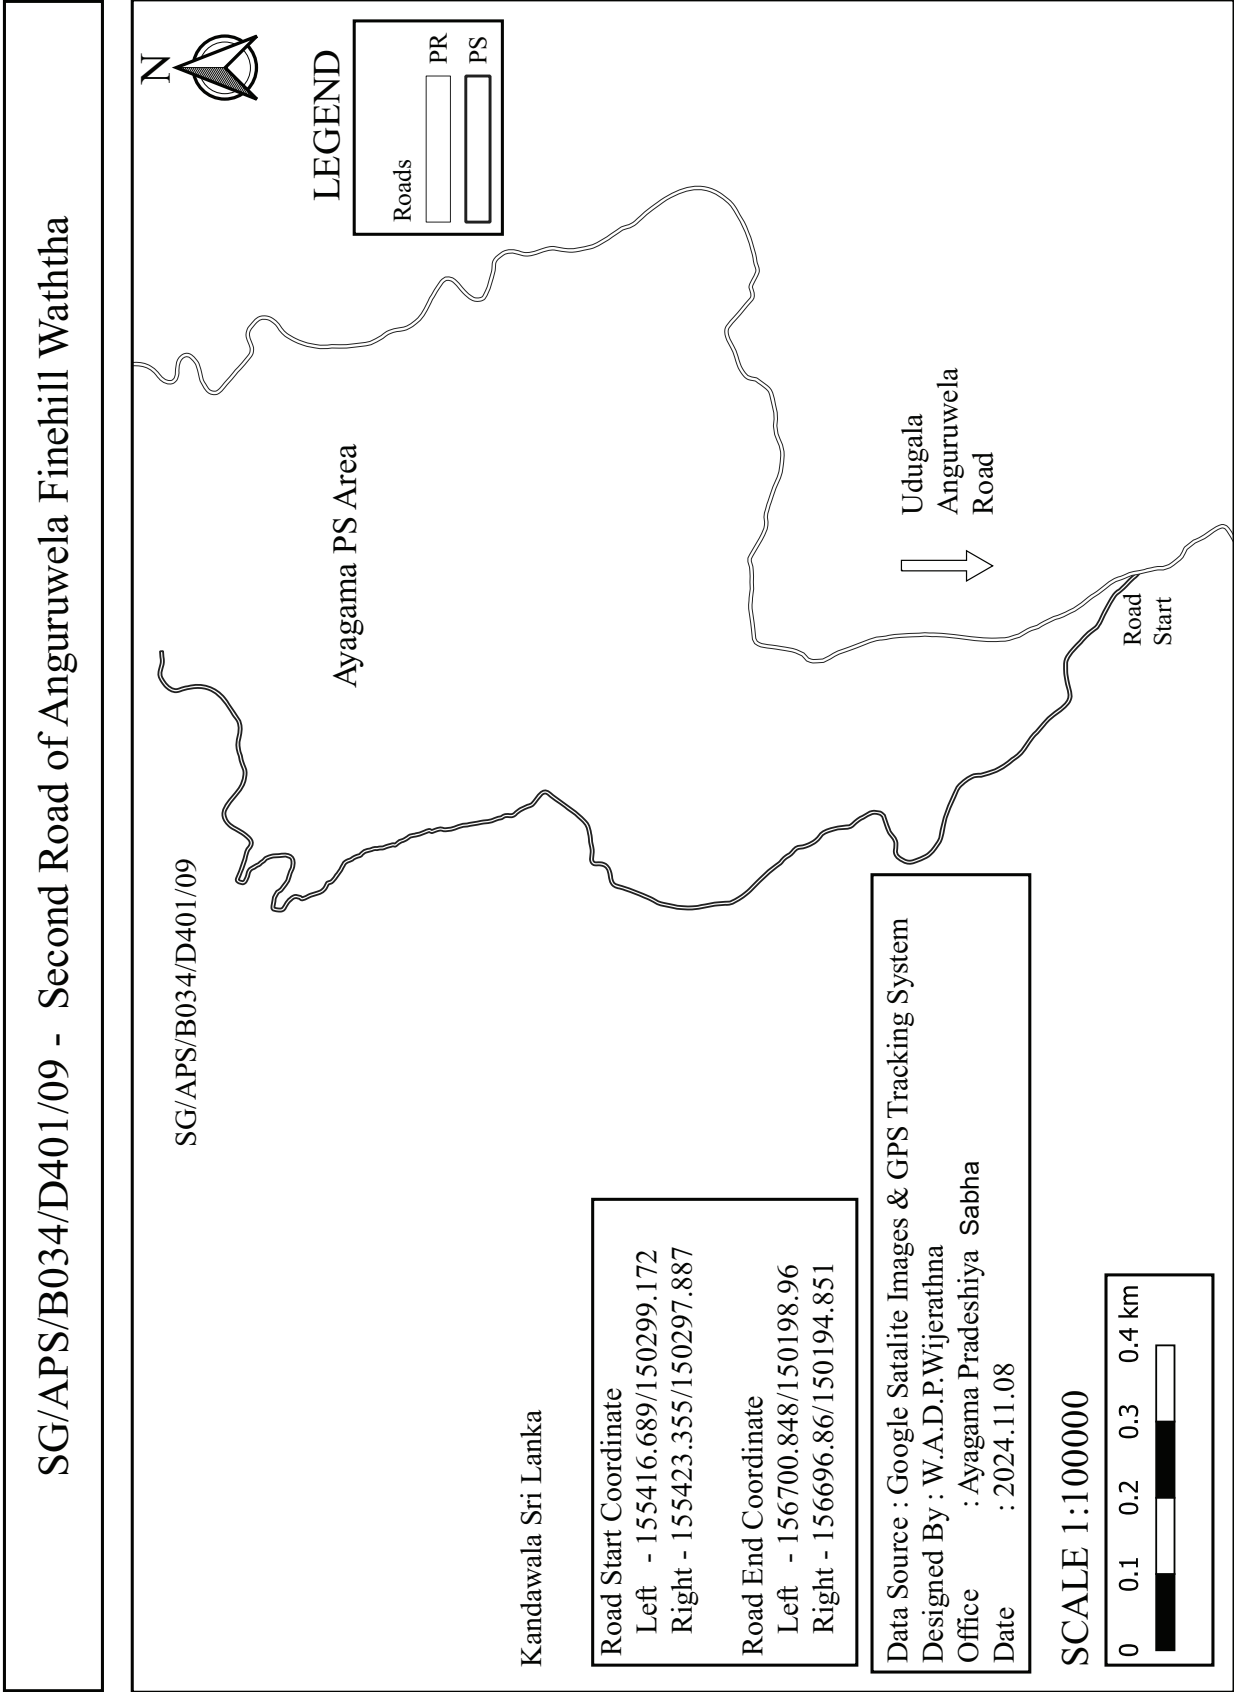


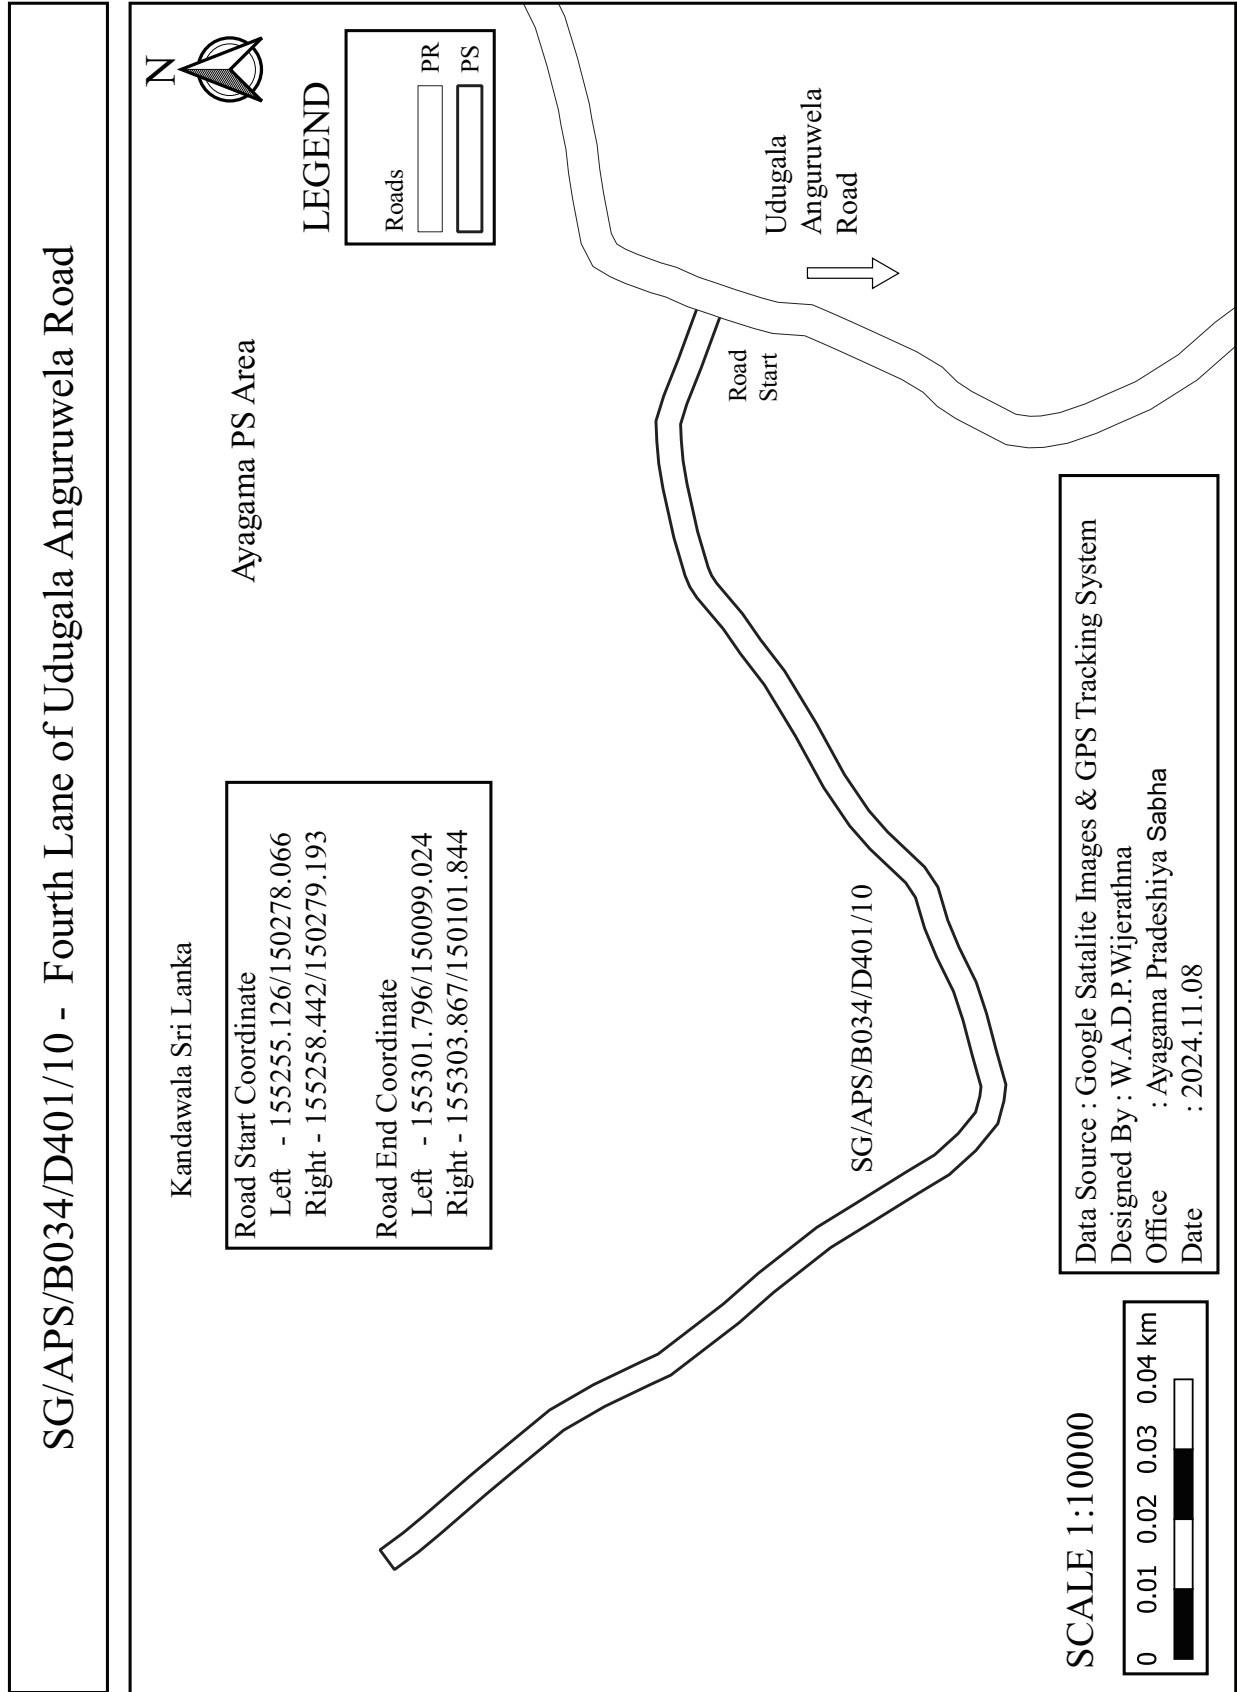


SG/APS/B034/D401/11 - Anguruwela Tank Footpath

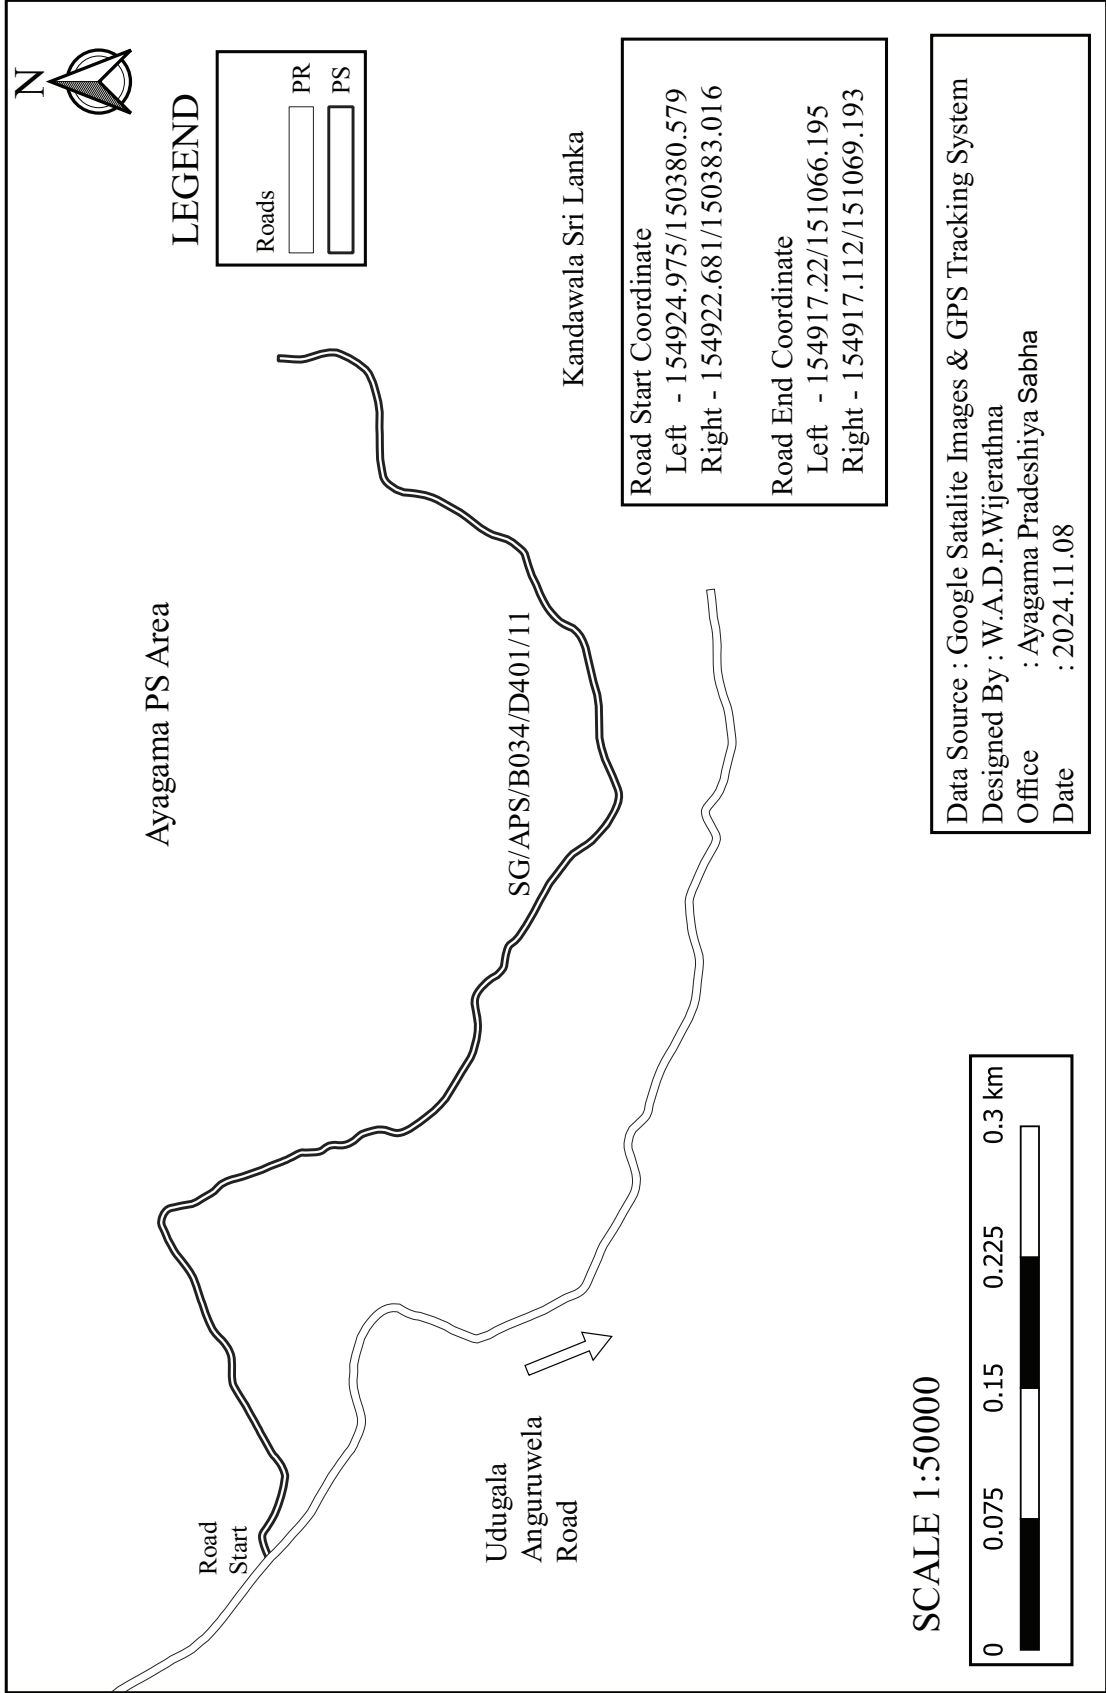



SG/APS/B034/D401/12 - First Lane of Panwilahena

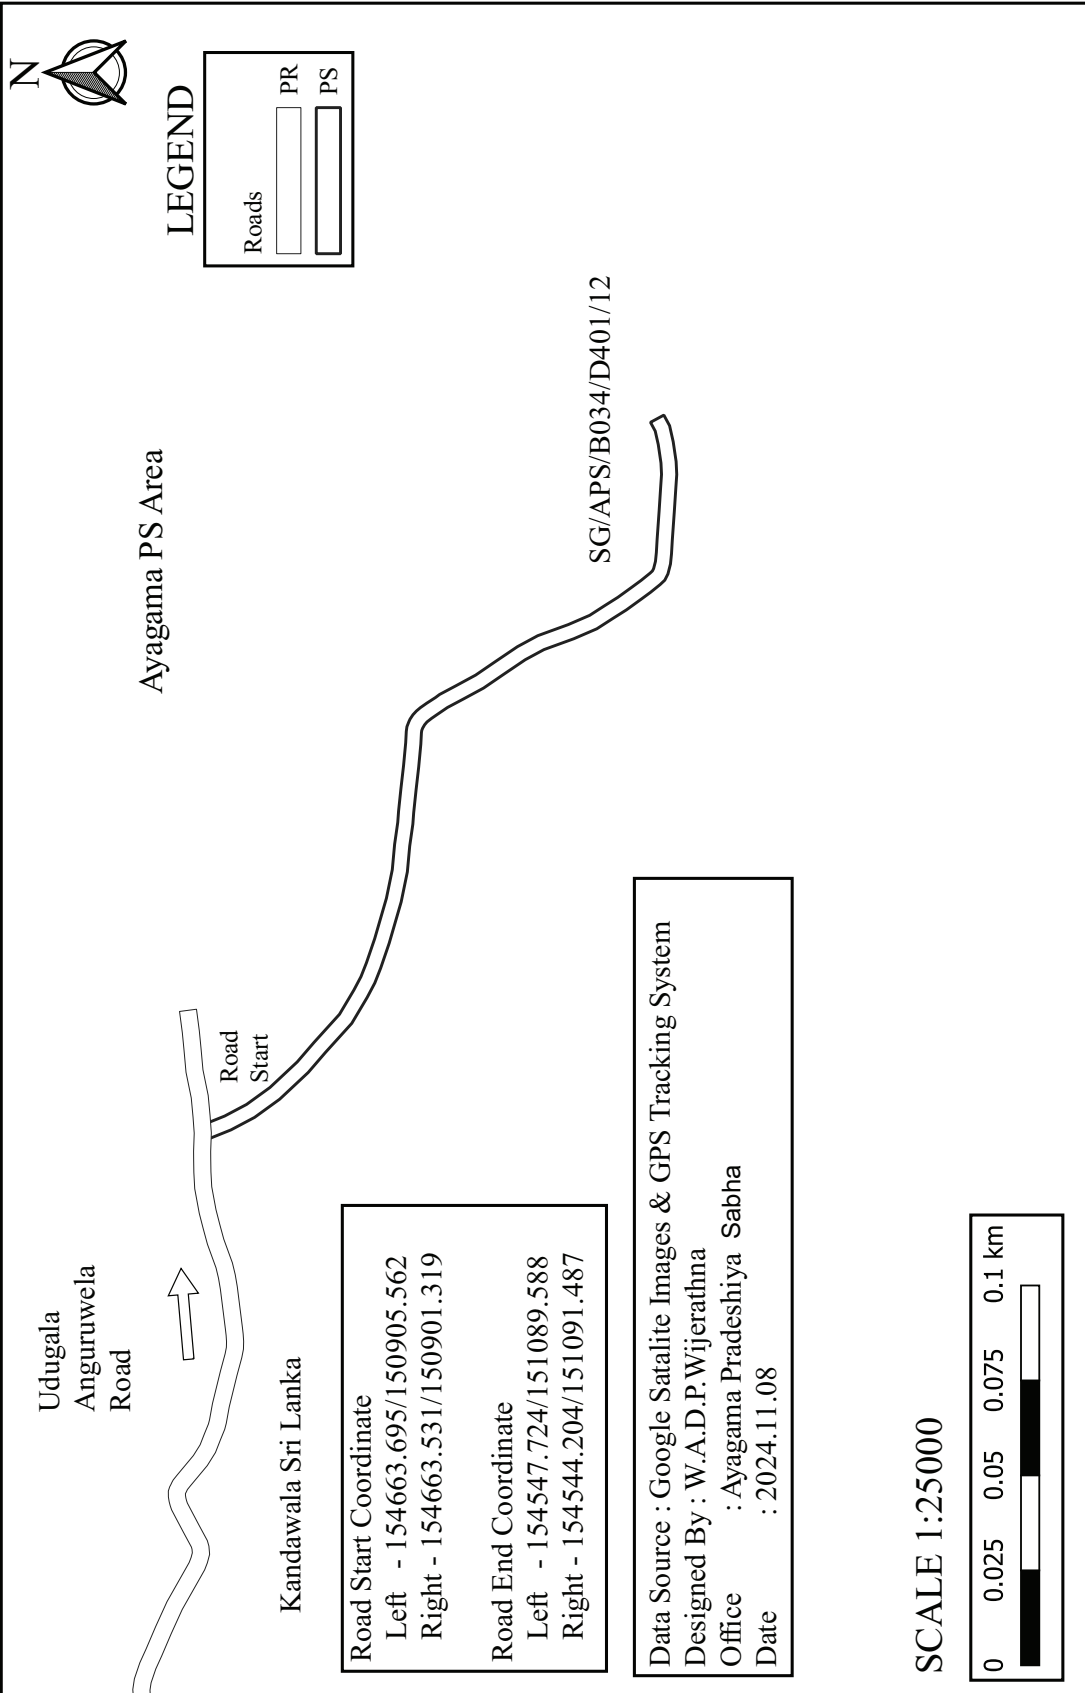



SG/APS/B034/D401/13 - Anguruwela Panwilahena Road

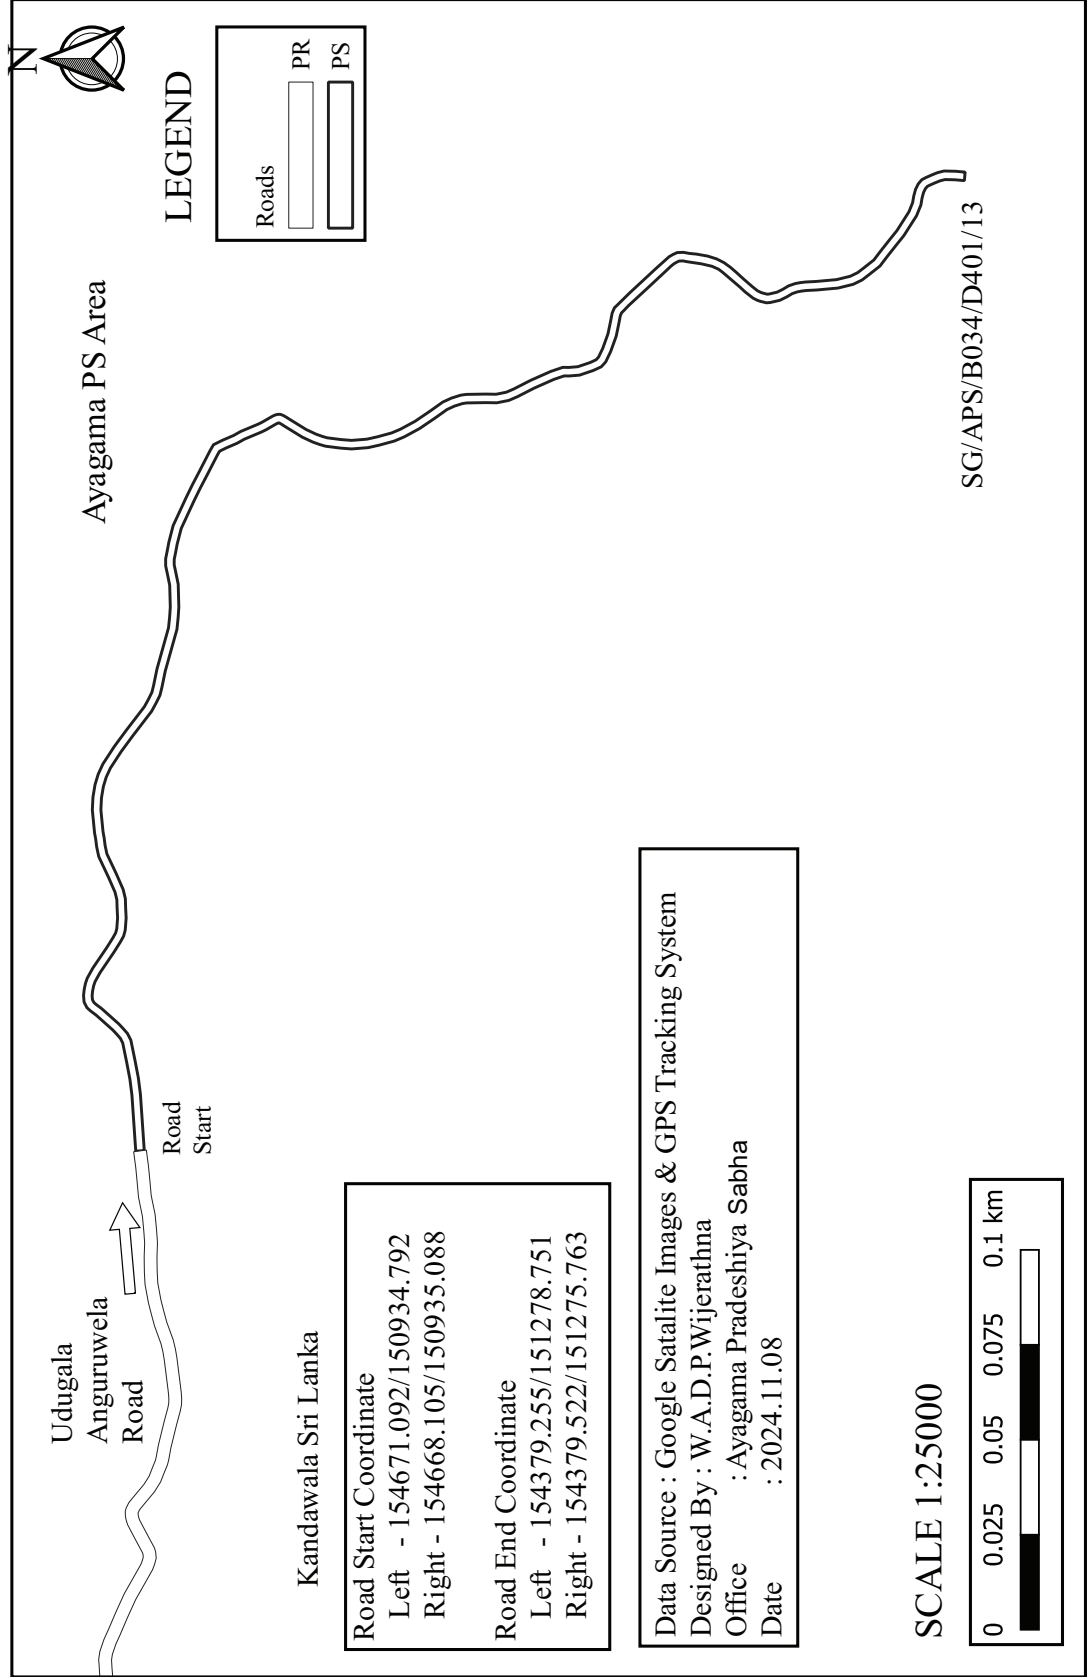


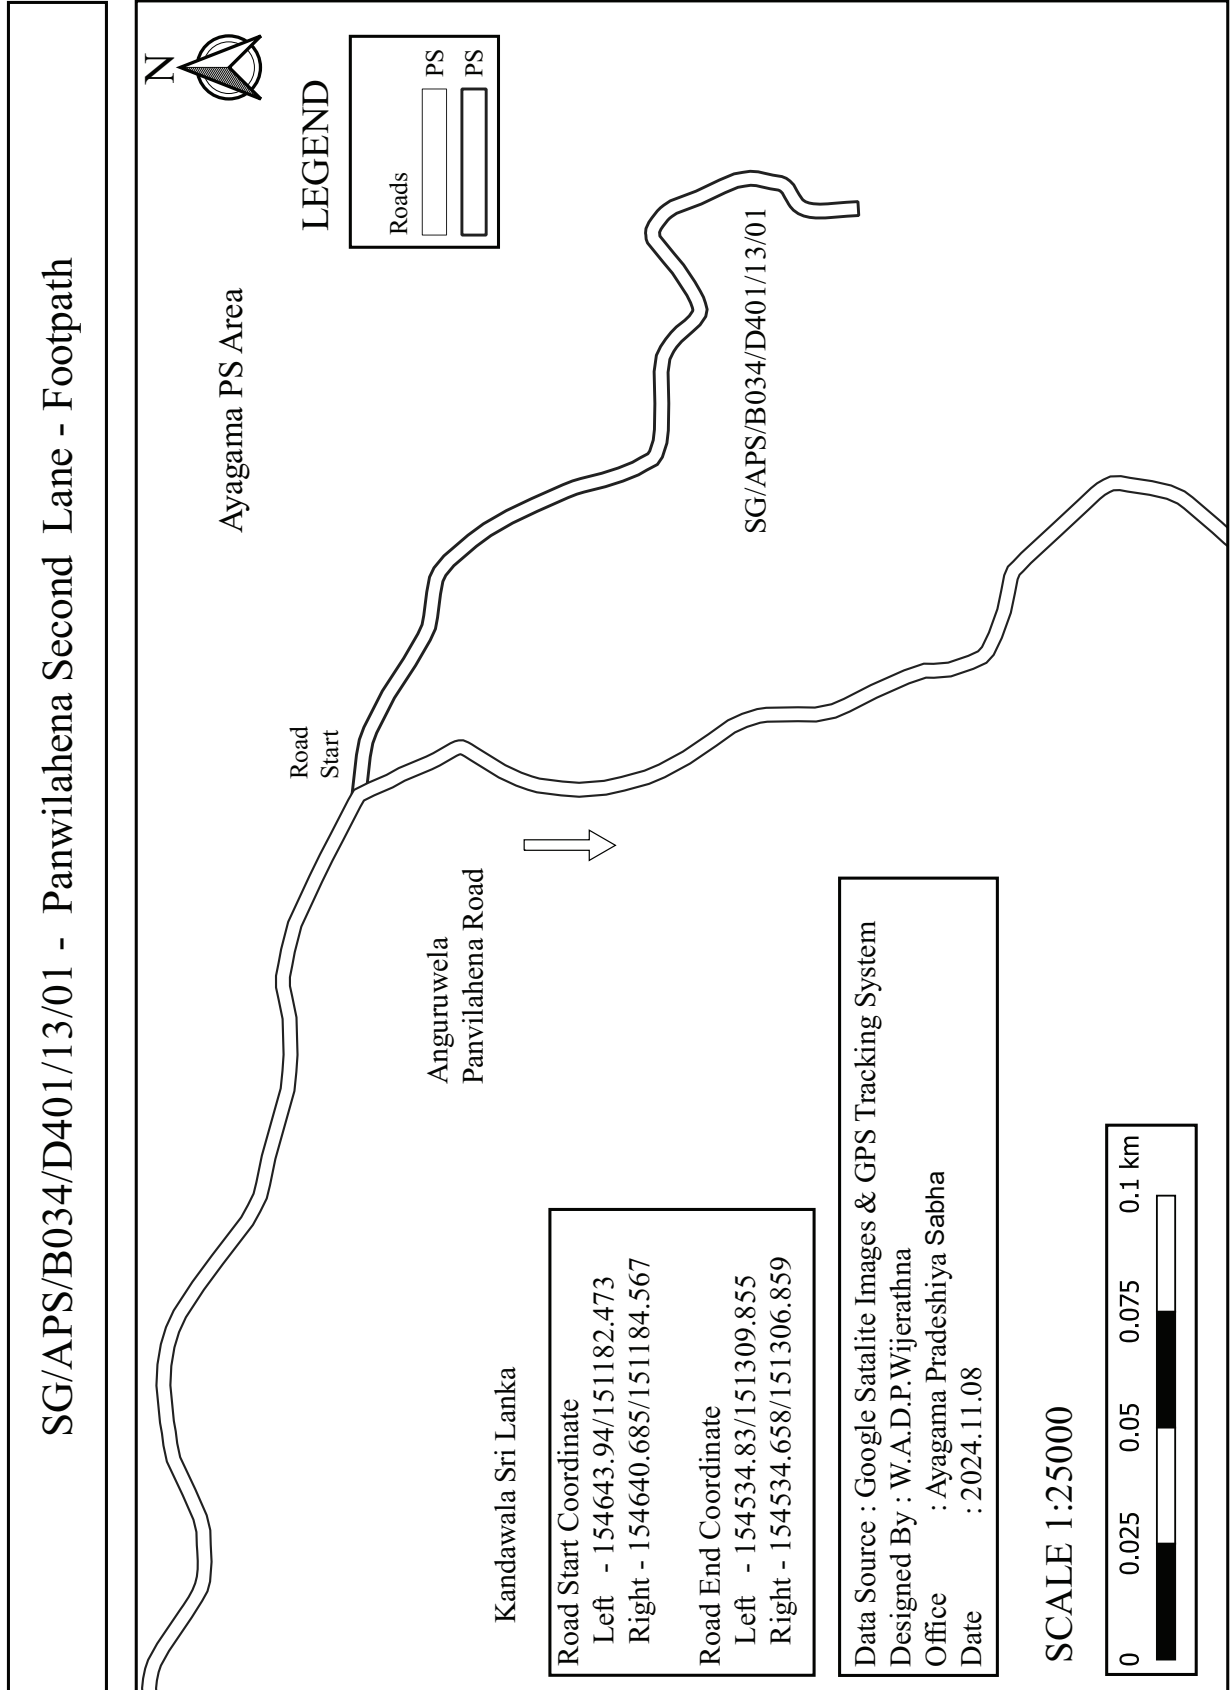

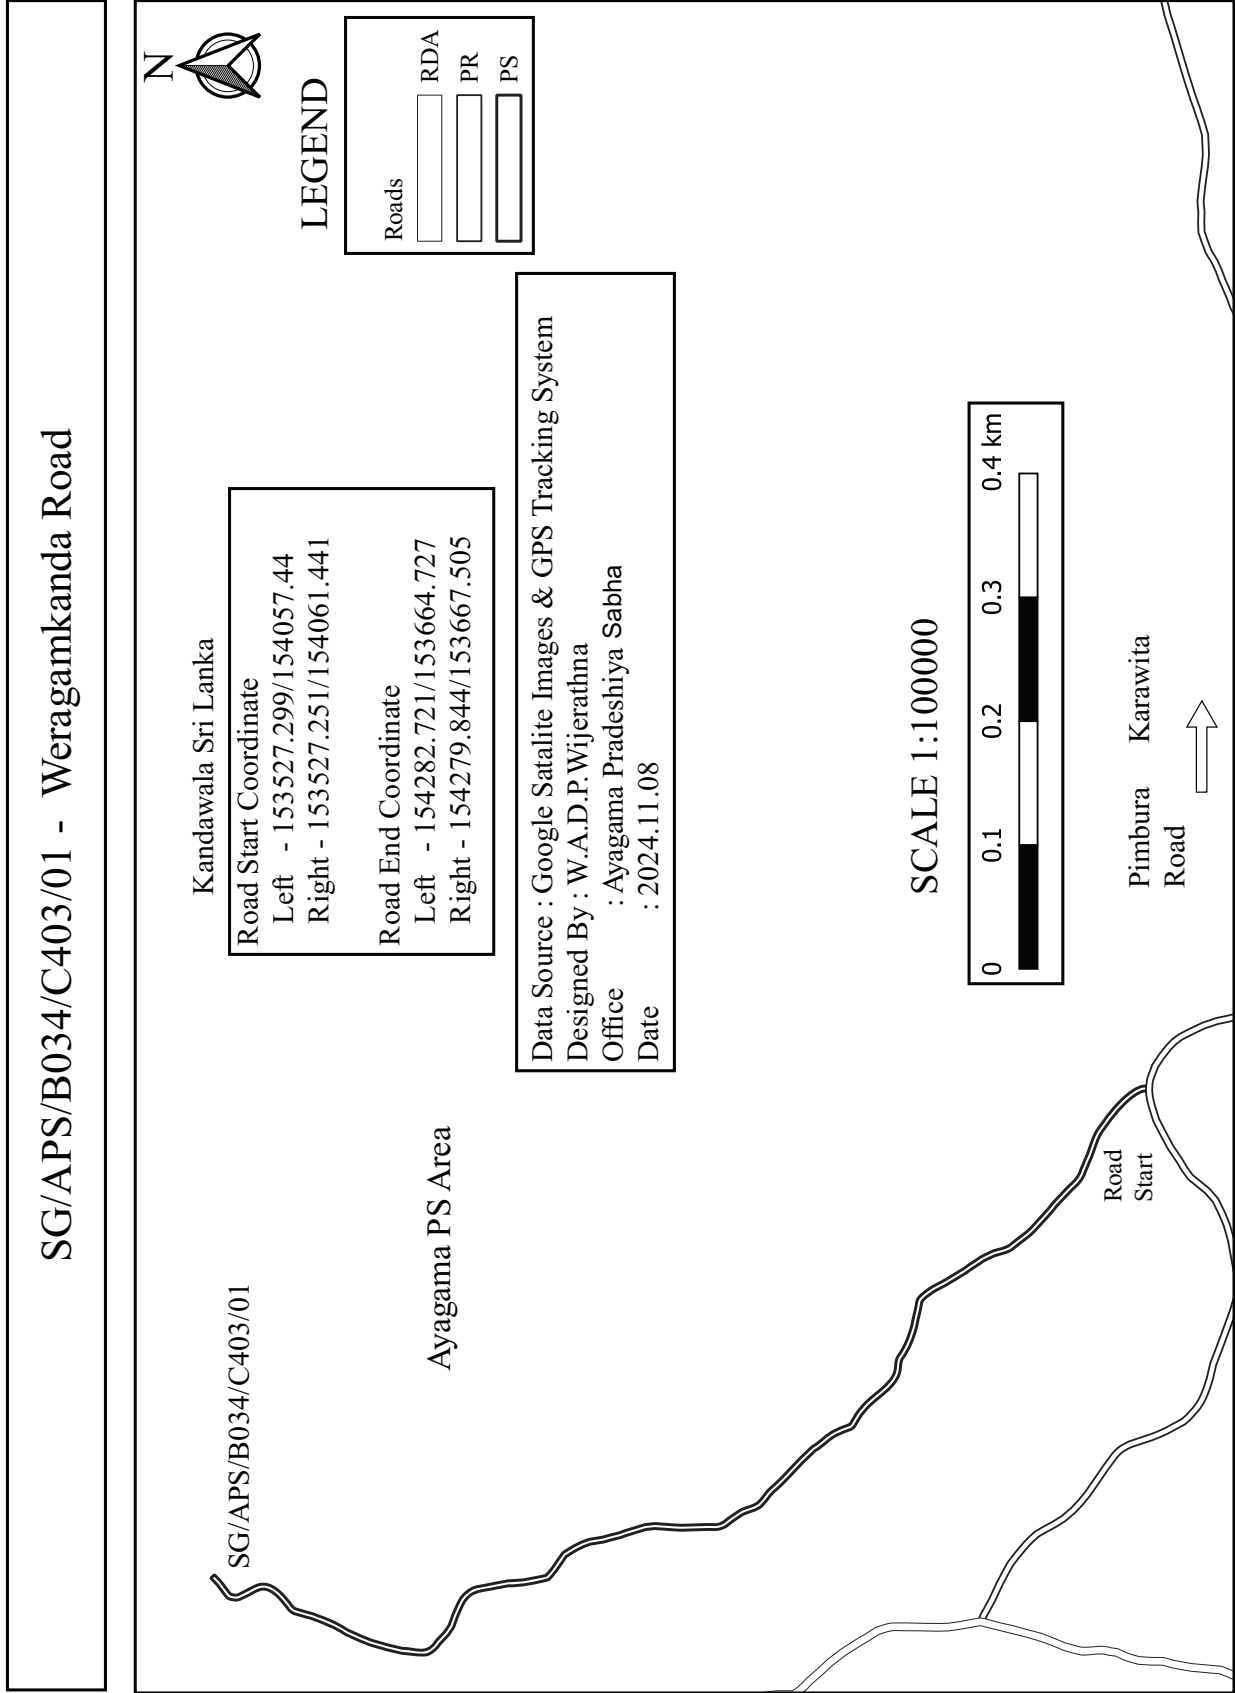

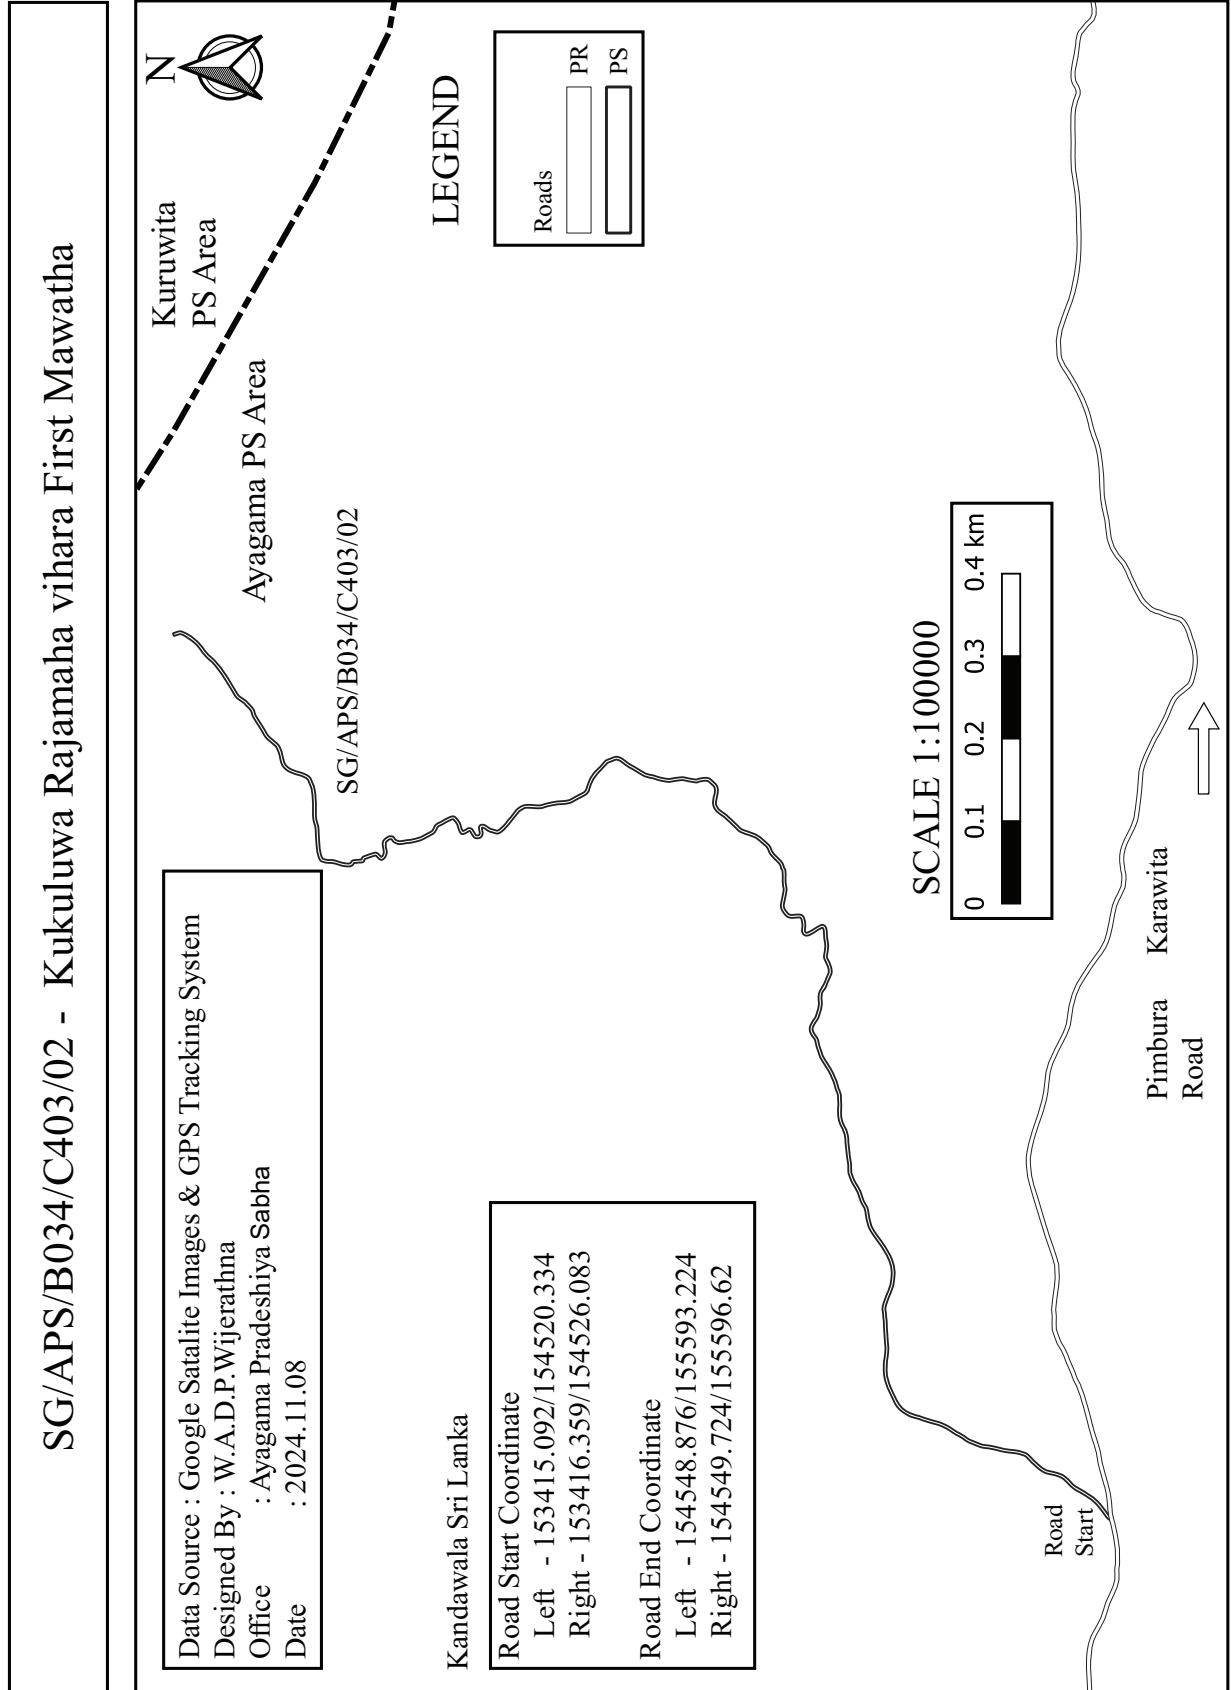

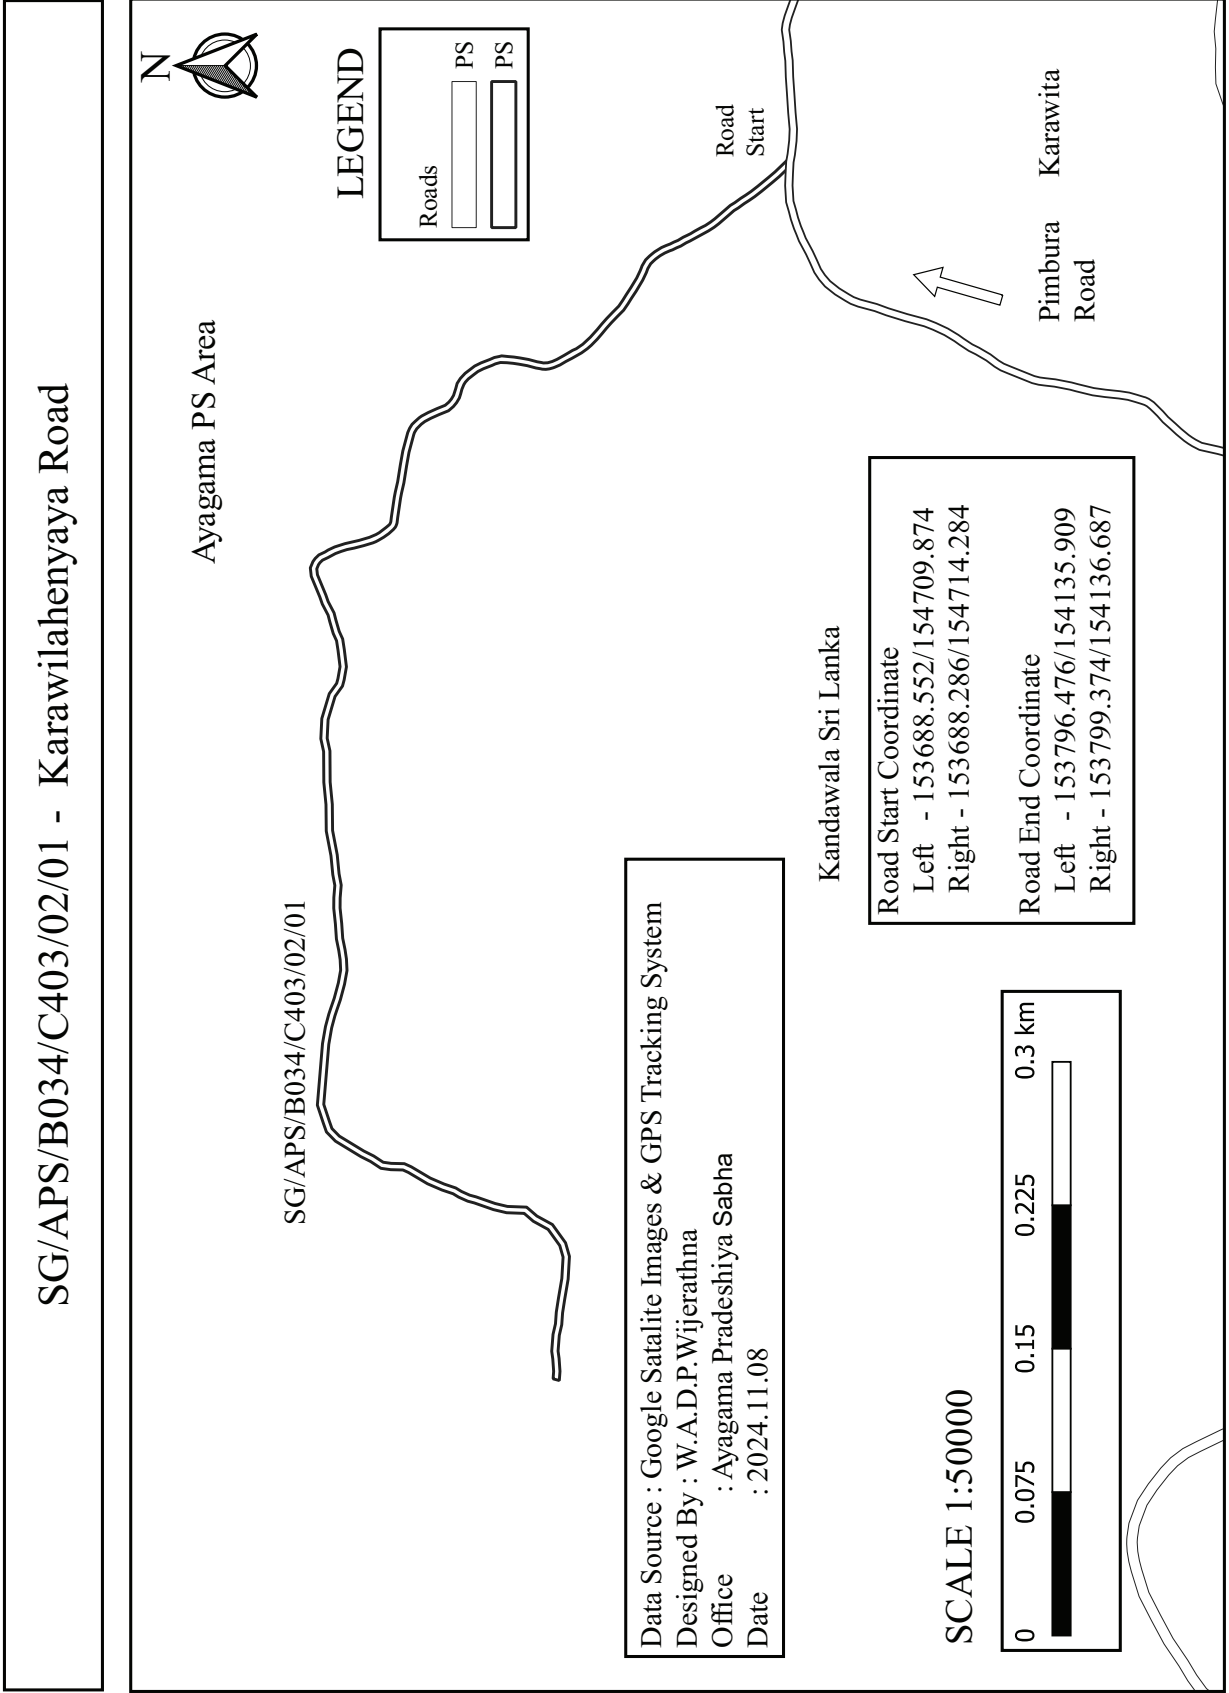

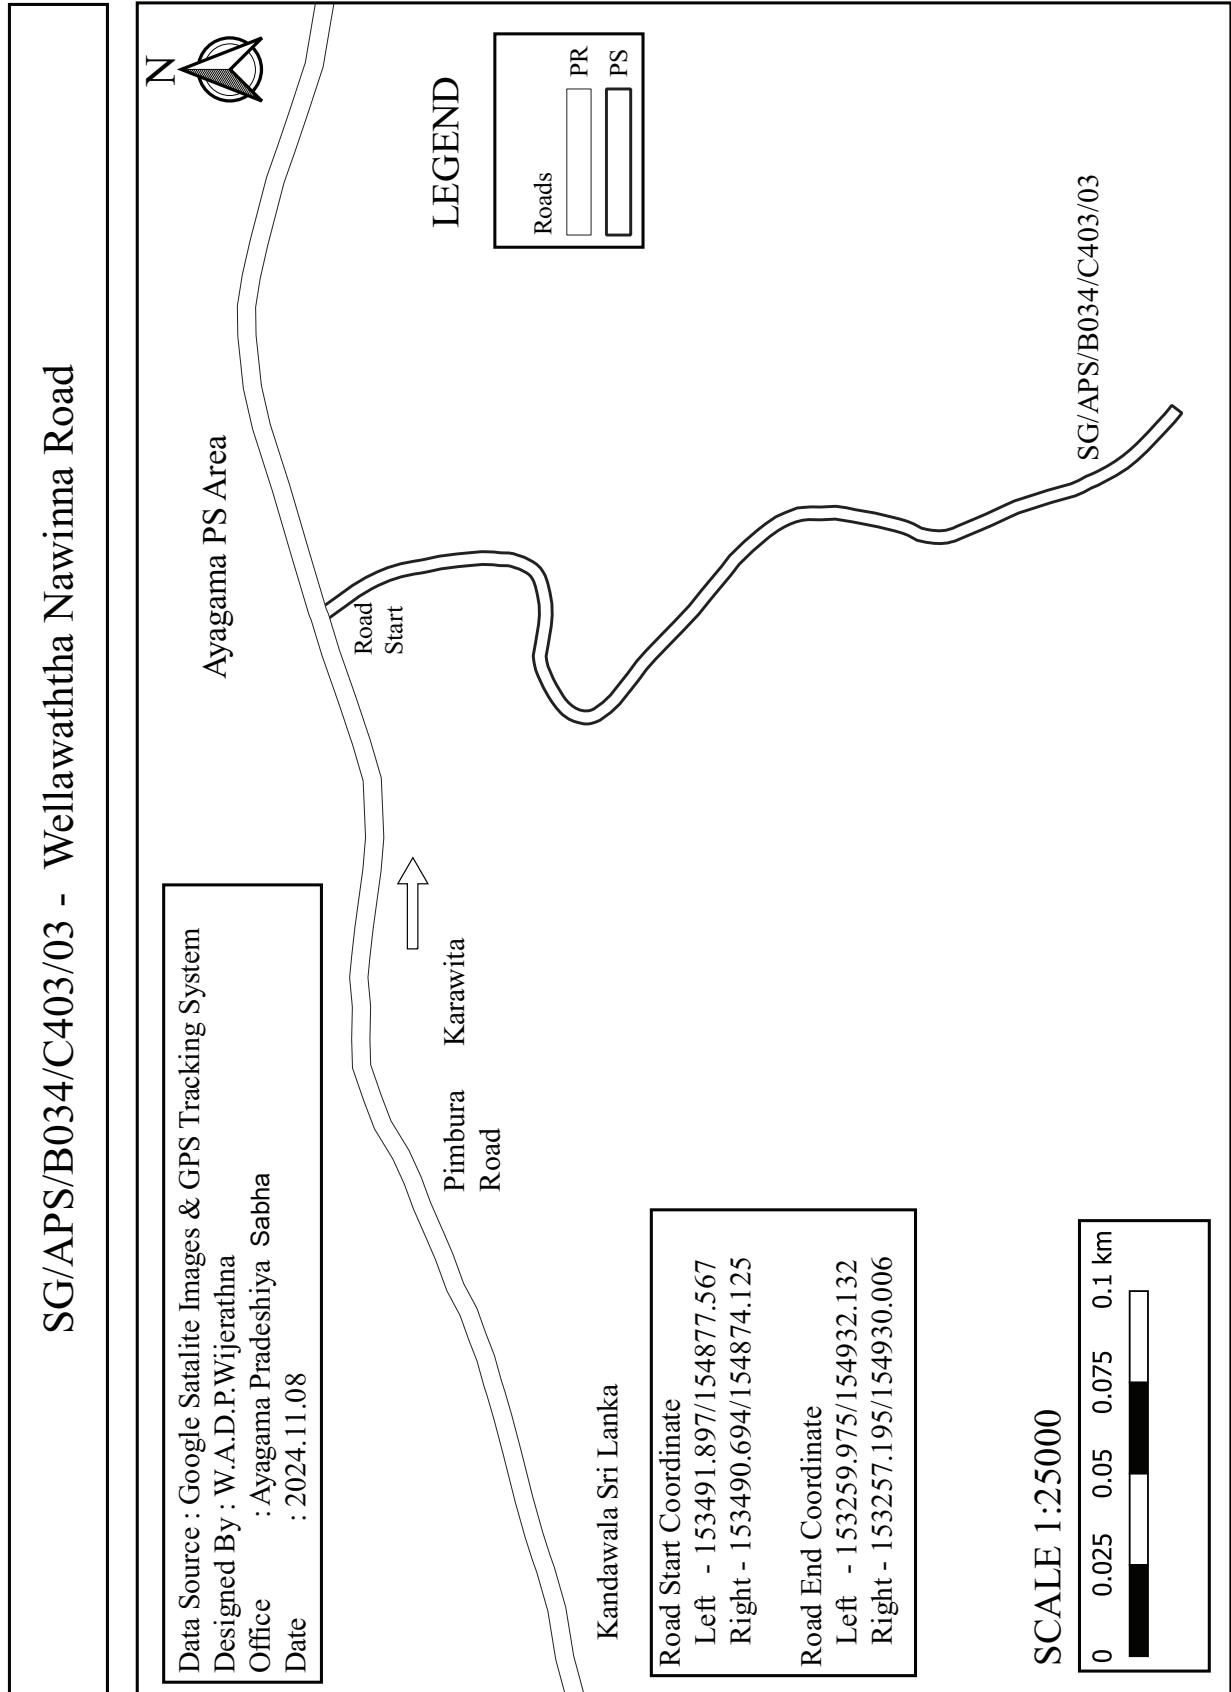

SG/APS/B034/C403/04 - Kukuluwa Rajamaha Vihara Footpath

Data Source : Google Satalite Images & GPS Tracking System
 Designed By : W.A.D.P.Wijerathna
 Office : Ayagama Pradeshiya Sabha
 Date : 2024.11.08



Ayagama PS Area

LEGEND


Roads	PR	PS

SG/APS/B034/C403/04

Kandawala Sri Lanka

Road Start Coordinate
 Left - 153515.858/154959.691
 Right - 153515.612/154961.225
 Road End Coordinate
 Left - 153738.21/155002.228
 Right - 153738.768/155003.684


SCALE 1:25000

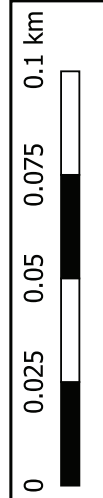

Road Start

Pimbura Road
 Karawita



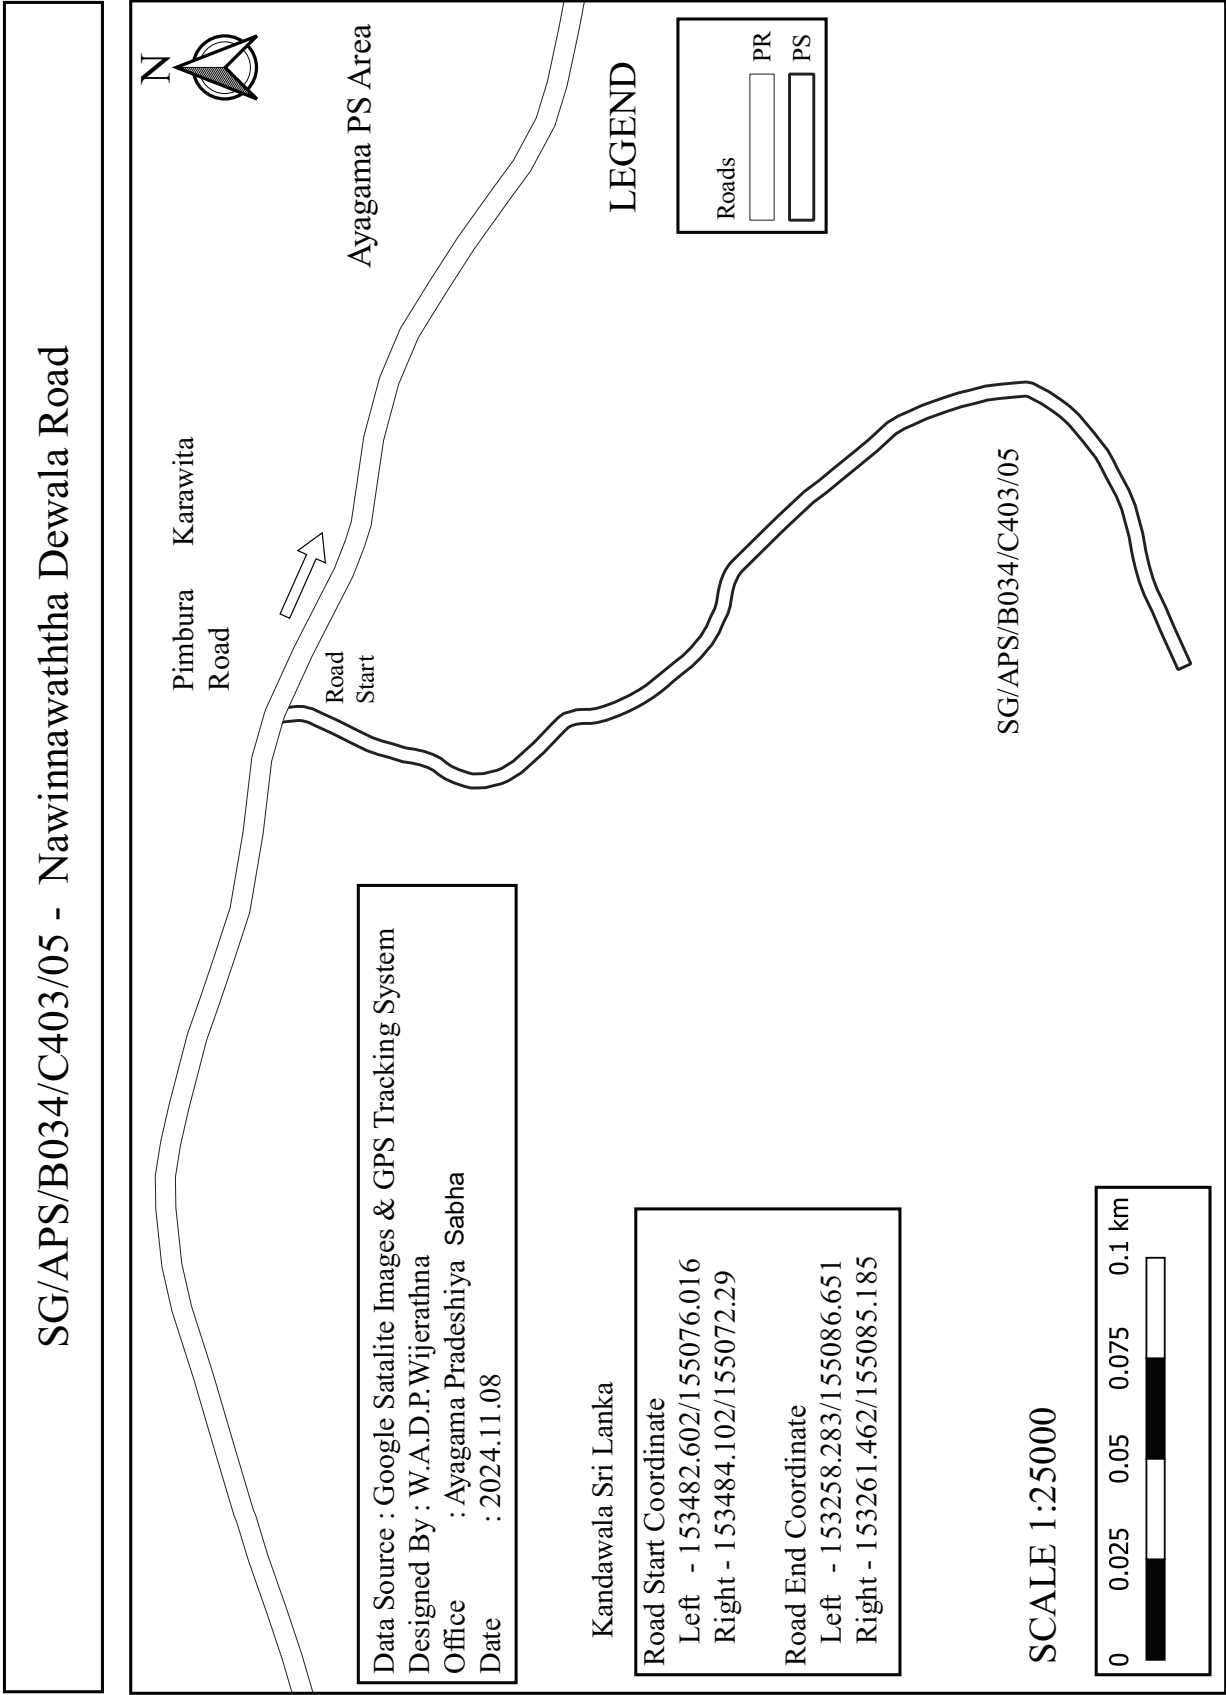

SG/APS/B034/C403/06 - Nawinnawaththa Kurahana Road

