



ශ්‍රී ලංකා ප්‍රජාතාන්ත්‍රික සමාජවාදී ජනරජයේ ගැසට් පත්‍රය

අති විශේෂ

අංක 2414/05 - 2024 දෙසැම්බර් මස 10 වැනි අඟහරුවාදා - 2024.12.10

(රජයේ බලයට ප්‍රසිද්ධ කරන ලදී)

IV (අ) වැනි කොටස - පළාත් පාලනය

පළාත් පාලන නිවේදන

අයගම ප්‍රාදේශීය සභාව

1987 අංක 15 දරන ප්‍රාදේශීය සභා පනතේ 24 වන වගන්තිය සමග කියවිය යුතු, සබරගමුව පළාතේ ගරු ආණ්ඩුකාරතුමා විසින් අංක 2316/20 සහ 2023 ජනවාරි මස 24 වැනි දිනැති අති විශේෂ ගැසට් පත්‍රයේ ප්‍රකාශයට පත්කරනු ලැබ ඇති "සබරගමුව පළාතේ ප්‍රාදේශීය සභා විසින් පවත්වාගෙන යනු ලබන පාරවල් හා පටු මාවත්වල සැලසුම් පිළියෙළ කිරීම හා නාම ලේඛනය දක්වමින් දැන්වීම් පළ කිරීම පිළිබඳ නියෝග" මාලාවෙන් සබරගමුව පළාතේ ප්‍රාදේශීය සභාවලට පවරා දී ඇති කාර්යය අනුව, මෙහි පහත උපලේඛනයේ ඇතුළත් පාරවල් සහ පටු මාවත් අයගම ප්‍රාදේශීය සභාව සතු වී ඇති පාරවල් සහ පටු මාවත් වශයෙන් ප්‍රකාශයට පත් කළ යුතු බව 2024.06.20 දින පවත්වනු ලැබූ සභා රැස්වීමේ අංක 03 යටතේ තීරණය කරනු ලැබ ඇති බව මහජනතාවගේ දැන ගැනීම සඳහා මෙයින් ප්‍රසිද්ධ කරනු ලැබේ.

එකී උපලේඛනයේ ඇතුළත් යම් පාරක් හෝ පටු මාවතක් කිසියම් ඉඩමක් හරහා හෝ යම් ඉඩමක කොටසකට ඇතුළත් වන බව, ඒ ඉඩමට හිමිකම් කියනු ලබන පාර්ශවයේ මතය වේ නම්, එකී ඉඩමට තමන්ගේ ඇති අයිතිය ඔප්පු කිරීම සඳහා මෙම නිවේදනයේ දින සිට මාස තුනක කාලයක් ඉකුත්වීමට පෙර නිසි අධිකරණයේ නඩුවක් පැවරීමට ක්‍රියා කළ යුතු බවත් මෙයින් නිවේදනය කරනු ලැබේ.

තවදුරටත් එසේම, එකී මාස තුනක කාලය අවසන් වීමට පෙර එවැනි නඩුවක් පවරා නැති එකී උපලේඛනයේ ඇතුළත් සෑම පාරක්ම සහ පටු මාවතක්ම අයගම ප්‍රාදේශීය සභාව සතු කරනු ලැබ ඇති පාරක් හෝ පටු මාවතක් ලෙස සලකනු ලබන බව වැඩිදුරටත් නිවේදනය කරනු ලැබේ.

කේ. ඒ. ඩී. එම්. කුඩාආරච්චි,
ලේකම් හා බලතල, කාර්ය කාර්යාල
ක්‍රියාත්මක කිරීමේ නිලධාරී,
අයගම ප්‍රාදේශීය සභාව.

2024 දෙසැම්බර් මස 05 වැනි දින,
අයගම ප්‍රාදේශීය සභාව,
අයගම.

අයගම කළමනාකරණ මාර්ගයට සම්බන්ධිත අයගම ප්‍රාදේශීය සභාවට අයත් මාර්ග නාමලේඛනය

අනු අංකය	පාලනික කේතය	පාර්ශ්ව නම	ආරම්භක බිත්තිය (කළමනාකරණ ලංකා)		අවසාන බිත්තිය (කළමනාකරණ ලංකා)		පාර්ශ්ව දිග (මීටර්)	පාර්ශ්ව පළල (මීටර්)	සංවර්ධන පළල (මීටර්)
			වම්	දකුණ	වම්	දකුණ			
1	SG/APS/B034/01	පැළලිමොදුරුවත්ත මාර්ගය	159876.947/148983.413	159874.112/148984.555	159905.907/149885.744	159906.975/149882.939	1352.2	3.0	2.5
2	SG/APS/B034/01/01	පැළලිමොදුරුවත්ත ගම්පහ මාර්ගය	159877.497/149042.944	159878.751/149049.381	160030.782/149513.286	160027.886/149512.507	602.81	3.0	2.5
3	SG/APS/B034/02	අයගම අක්කර 08 යකඳුවෙල මාර්ගය	159776.853/149052.16	159779.998/149049.682	160468.738/147891.991	160465.818/147894.809	1857.53	4.0	3.0
4	SG/APS/B034/02/01	මහපොරොත්තු මාර්ගය	159735.011/149000.084	159735.439/148996.823	159373.122/148527.286	159375.522/148525.486	784.49	3.0	2.0
5	SG/APS/B034/02/02	වැරදියකැටිය මාර්ගය	159881.887/148705.505	159880.342/148701.478	159569.287/148483.953	159571.939/148486.947	529.65	4.0	2.5
6	SG/APS/B034/02/02/01	වැරදියකැටිය මාර්ගයේ පළමු දෙවන පටුම	159700.651/148621.953	159697.668/148622.287	159689.727/148674.064	159686.763/148674.528	58.83	3.0	2.8
7	SG/APS/B034/02/02/02	වැරදියකැටිය මාර්ගයේ දෙවන පටුම	159676.864/148629.875	159670.766/148631.369	159648.827/148658.334	159645.965/148659.235	46.61	3.0	3.0
8	SG/APS/B034/02/03	අක්කර 08 මාර්ගය	159896.163/148288.035	159893.565/148284.896	159044.8/148734.409	159043.773/148730.109	993.24	4.0	3.5
9	SG/APS/B034/02/04	වත්තලත්තකන්ද පහළ මාර්ගය	159879.35/148221.045	159877.375/148218.784	159479.305/148252.167	159476.739/148250.614	422.79	3.0	2.7
10	SG/APS/B034/02/05	අක්කර 08 වත්තලත්තකන්ද මාර්ගය	159863.257/148197.441	159863.872/148193.483	159857.93/147900.482	159859.376/147904.212	435.75	4.0	3.0
11	SG/APS/B034/02/05/01	අක්කර 08 වත්තලත්තකන්ද මාර්ගයේ පළමු පටුම	159717.39/148002.043	159718.897/147999.446	159572.467/147803.659	159574.459/147799.764	258.78	3.0	2.0
12	SG/APS/B034/02/06	කිතුල්ල මාර්ගය	159927.749/148107.283	159930.172/148103.793	159847.958/148014.5	159851.903/148015.158	129.72	4.0	3.0
13	SG/APS/B034/02/07	වත්තලත්තකන්ද මාර්ගය	160406.523/147812.894	160410.882/147813.516	159301.816/147931.145	159305.283/147929.148	1514.7	4.0	3.5
14	SG/APS/B034/02/07/01	කැකුණගම මාර්ගය	160409.473/147806.227	160410.098/147810.406	160319.044/147126.992	160322.993/147126.359	1036.92	4.0	3.5
15	SG/APS/B034/02/07/02	සුනිමලාමය මාර්ගය	160275.603/147707.697	160279.735/147709.571	160452.02/147575.579	160454.159/147578.349	228.15	3.5	2.6

අනු අංකය	පාලනික කේතය	පාලන නම	ආරම්භක බණ්ඩාරක (කදවල ශ්‍රී ලංකා)		අවසාන බණ්ඩාරක (කදවල ශ්‍රී ලංකා)		පාලන දින (මිටර්)	පාලන සාමාන්‍ය පළල (මිටර්)	සංවර්ධිත පළල (මිටර්)
			වම	දකුණ	වම	දකුණ			
16	SG/APS/B034/02/07/03	වත්තඉන්නකන්ද මාර්ගයේ පළමු පටුම	160123.442/147596.918	160124.761/147599.693	160270.834/147498.315	160271.575/147501.222	192.95	3.0	3.0
17	SG/APS/B034/02/07/04	මල්වෙල අතුරු අඩිපාර	160115.296/147583.669	160117.421/147586.06	160080.563/147501.059	160083.058/147499.39	116.49	3.0	2.0
18	SG/APS/B034/02/07/05	වත්තඉන්නකන්ද කැකුණෙ හමන් මාර්ගය	160029.201/147534.248	160032.641/147535.317	160417.467/147281.162	160415.341/147284.577	520.85	3.5	3.0
19	SG/APS/B034/03	පඬු මෙවදා නිලධාරී කාර්යාල මාර්ගය	159683.217/149143.266	159678.225/149151.754	159574.286/149243.05	159578.091/149243.562	217.39	4.0	3.0
20	SG/APS/B034/04	නිහතමානිම සමරුමම තොරණගොඩ මාර්ගය	159499.955/149200.61	159496.052/149199.269	159377.076/149566.606	159379.326/149570.003	1401.66	4.0	3.5
21	SG/APS/B034/04/01	සරත්පුරය පළමු පටුම	159471.165/149219.603	159466.88/149220.591	159469.014/149295.972	159465.021/149295.734	72.66	4.0	3.0
22	SG/APS/B034/04/02	සරත්පුරය දෙවන පටුම	159392.077/149223.459	159390.157/149224.139	159356.266/149288.908	159352.841/149289.672	128.52	2.0	1.0
23	SG/APS/B034/04/03	කොටුවවත්ත මාර්ගය	159250.253/149314.197	159256.987/149315.207	159249.113/149289.054	159251.528/149289.703	40.35	2.5	2.0
24	SG/APS/B034/04/04	සරත්පුරය සිට සුසානගුමිය දක්වා මාර්ගය	159117.957/149522.031	159116.825/149524.857	159275.288/149566.638	159273.2/149568.792	187.03	3.0	3.0
25	SG/APS/B034/04/05	නිහතමානිම පහළ වතු මාර්ගය	159058.681/149552.921	159061.605/149551.934	159020.189/149590.958	159018.534/149593.463	460.36	3.0	3.0
26	SG/APS/B034/04/06	නිහතමානිම බෙරලියන මාර්ගය	158983.715/149677.2	158982.347/149673.256	158383.276/149913.921	158381.918/149910.023	833.08	4.0	3.5
27	SG/APS/B034/04/06/01	මහමන්න වත්ත මාර්ගය	158964.351/149692.745	158961.299/149694.296	158998.977/150099.954	158996.351/150101.403	544.1	3.0	3.0
28	SG/APS/B034/04/07	සමරුමම සුසානගුමි මාර්ගය	159222.068/149663.818	159222.56/149662.789	159167.768/149577.524	159169.575/149577.603	109.07	1.0	1.0
29	SG/APS/B034/05	අක්කර 17 මාර්ගය	159211.519/149034.985	159218.216/149030.927	159041.303/148733.53	159047.967/148731.88	414.34	4.0	3.0
30	SG/APS/B034/05/01	අක්කර 17 මාර්ගයේ පළමු පටුම	159130.998/148885.536	159127.121/148884.22	159083.254/148926.653	159080.254/148924.85	66.63	3.5	3.0
31	SG/APS/B034/05/02	අක්කර 17 උඩුවත්තන්ද මාර්ගය	159044.8/148734.409	159043.773/148730.109	158125.354/149478.274	158121.421/149477.302	1973.6	4.0	3.0

අනු අංකය	පාලනික කේතය	පාරේ නම	ආරම්භක බණ්ඩාංක (කදවල ශ්‍රී ලංකා)		අවසාන බණ්ඩාංක (කදවල ශ්‍රී ලංකා)		පාරේ දිග (මීටර්)	පාරේ සාමාන්‍ය පළල (මීටර්)	සංවර්ධිත පළල (මීටර්)
			වම	දකුණ	වම	දකුණ			
32	SG/APS/B034/05/02/01	අක්කර 17 උඩුවක්කන්ද මාර්ගයේ පළමු පටුම	159021.748/148734.947	159025.062/148734.705	158796.759/148656.29	158795.047/148653.825	470.44	3.0	2.0
33	SG/APS/B034/05/02/01/01	අක්කර 17 උඩුවක්කන්ද මාර්ගයේ පළමු පටුමගෙහි පළමු අතුරු මාර්ගය	158991.422/148548.772	158992.385/148549.052	159057.796/148519.906	159058.97/148519.778	84.02	1.0	1.0
34	SG/APS/B034/05/02/02	අක්කර 17 බලිගල තලපක්ගල මාර්ගය	158790.021/148650.333	158794.837/148653.525	158382.198/147780.059	158385.922/147778.599	1370.58	4.0	3.0
35	SG/APS/B034/05/02/02/01	අක්කර 17 බලිගල තලපක්ගල මාර්ගයේ පළමු පටුම	158817.423/148519.898	158817.439/148528.493	158838.804/148127.09	158822.184/148132.745	639.36	4.0	3.0
36	SG/APS/B034/05/02/03	අක්කර 17 උඩුවක්කන්ද මාර්ගයේ දෙවන පටුම	158438.414/148763.884	158435.909/148765.709	158503.197/148862.357	158500.647/148860.779	128.87	3.0	3.0
37	SG/APS/B034/06	ඇරපොරුල් පළමු මාර්ගය	158948.58/149198.35	158950.482/149197.656	158925.977/149044.689	158927.188/149046.282	175.85	2.0	2.0
38	SG/APS/B034/07	තංගුල්ල ඇරපොරුල් මාර්ගය	158756.919/149280.358	158751.859/149280.624	158853.235/149666.474	158851.455/149670.328	493.5	4.0	3.0
39	SG/APS/B034/08	බතලවත්ත මාර්ගය	158734.228/149276.134	158737.683/149275.567	159079.02/148828.925	159080.342/148832.184	641.26	3.5	3.0
40	SG/APS/B034/09	බොරැයන නැගිටිකන්ද මාර්ගය	158343.692/149536.821	158333.851/149536.613	157532.409/151660.94	157528.419/151661.227	3194.99	4.0	3.0
41	SG/APS/B034/09/01	බොරැයන නැගිටිකන්ද මාර්ගයේ පළමු පටුම	158588.658/150216.398	158590.104/150219.052	158692.325/150185.096	158693.417/150187.89	110.23	3.0	2.0
42	SG/APS/B034/09/02	බොරැයන නැගිටිකන්ද මාර්ගයේ දෙවන පටුම	158627.329/150277.199	158626.656/150280.344	158689.683/150433.452	158692.408/150432.198	351.56	3.0	3.0
43	SG/APS/B034/09/03	බොරැයන නැගිටිකන්ද මාර්ගයේ තෙවන පටුම	158111.976/150987.353	158112.465/150991.438	158275.157/151205.948	158271.209/151206.585	306.03	4.0	3.0
44	SG/APS/B034/09/03/01	බොරැයන නැගිටිකන්ද මාර්ගයේ තෙවන පටුමගෙහි පළමු අතුරු මාර්ගය	158154.744/150992.508	158156.61/150997.015	158299.236/150956.415	158301.233/150959.881	161.88	4.0	3.0
45	SG/APS/B034/09/04	බොරැයන නැගිටිකන්ද මාර්ගයේ සිව්වන පටුම	157834.276/151232.737	157836.717/151228.902	157712.493/151213.456	157714.3/151209.888	141.11	4.0	4.0
46	SG/APS/B034/09/05	බොරැයන නැගිටිකන්ද මාර්ගයේ පස්වන පටුම	157738.073/151409.432	157739.279/151405.489	157651.773/151359.443	157651.821/151355.433	103.89	4.0	4.0

අනු අංකය	පාලනික කේතය	පාලන නම	ආරම්භක බණ්ඩාරක (කදවල ශ්‍රී ලංකා)		අවසාන බණ්ඩාරක (කදවල ශ්‍රී ලංකා)		පාලන දින (මිටර)	පාලන සාමාන්‍ය පළල (මිටර)	සංවර්ධිත පළල (මිටර)
			වම	දකුණ	වම	දකුණ			
47	SG/APS/B034/09/06	මෙරළියන නැගිටිකන්ද මාර්ගයේ පස්වන පටුම	157740.857/151414.172	157738.739/151412.038	157645.585/151601.7	157643.157/151603.606	236.88	3.0	3.0
48	SG/APS/B034/10	මදනගොඩ සිට උඩුගල දක්වා මාර්ගය	158181.837/149530.177	158184.494/149528.738	157391.423/149936.971	157396.102/149933.757	1022.88	3.0	3.0
49	SG/APS/B034/10/01	මදනගොඩ සිට උඩුගල දක්වා මාර්ගයේ පළමු පටුම	158011.146/149532.548	158013.627/149532.226	158005.128/149421.695	158007.541/149422.344	137.14	2.5	2.5
50	SG/APS/B034/10/02	පරලල මීට්ට පළමු පටු මාර්ගය	157873.215/149556.686	157875.354/149554.572	157702.551/149441.812	157700.574/149439.557	230.08	3.0	3.0
51	SG/APS/B034/10/02/01	පරලල මීට්ට පළමු පටු මාර්ගයේ අතුරු මාර්ගය	157863.022/149546.611	157866.471/149548.22	157875.338/149462.628	157875.905/149465.575	94.72	3.0	3.0
52	SG/APS/B034/10/03	පරලල මීට්ට දෙවන පටු මාර්ගය	157834.076/149624.615	157835.474/149621.555	157643.499/149637.885	157644.625/149635.105	203.97	3.0	3.0
53	SG/APS/B034/10/04	මදනගොඩ සිට උඩුගල දක්වා මාර්ගයේ දෙවන පටුම	157572.746/149848.72	157574.867/149848.169	157407.661/149823.444	157411.3/149823.103	209.54	2.0	2.0
54	SG/APS/B034/11	සිරිවර්ධනවත්ත පළමු මාර්ගය	158119.974/149611.359	158117.772/149613.678	158097.966/150266.167	158097.965/150269.167	797	3.0	3.0
55	SG/APS/B034/11/01	සිරිවර්ධනවත්ත පළමු මාර්ගයේ පළමු පටුම	158165.277/149982.886	158164.765/149979.875	158001.442/150157.23	158000.977/150154.266	278.05	3.0	3.0
56	SG/APS/B034/11/02	සිරිවර්ධනවත්ත පළමු මාර්ගයේ දෙවන පටුම	158183.877/150138.891	158183.701/150135.855	158056.203/150194.002	158054.299/150191.685	155.02	3.0	2.0
57	SG/APS/B034/12	සිරිවර්ධනවත්ත දෙවන මාර්ගය	158067.32/149668.969	158064.904/149672.168	158155.149/149764.095	158152.044/149766.619	132.98	4.0	3.7
58	SG/APS/B034/13	සිරිවර්ධනවත්ත කෙටි මාර්ගය	157819.709/149904.392	157818.331/149909.932	157908.052/149997.177	157909.043/150000.008	188.4	3.0	3.0
59	SG/APS/B034/14	කැකුළු මාර්ගය	157692.678/150117.011	157690.766/150120.01	157859.924/150207.02	157859.935/150210.02	209.84	3.0	2.5
60	SG/APS/B034/15	උඩුගල 700පන් මාර්ගය	157472.011/150400.013	157465.682/150409.027	158082.002/150937.345	158082.049/150940.482	1152.86	3.0	2.6
61	SG/APS/B034/16	උඩුගල සුසානතුම් මාර්ගය	157213.578/150638.917	157209.917/150640.688	157473.954/150759.872	157471.31/150762.871	441.99	4.0	3.0
62	SG/APS/B034/16/01	උඩුගල සුසානතුම් මාර්ගයේ පළමු පටුම	157441.317/150680.703	157443.508/150682.996	157490.669/150671.598	157491.717/150674.145	55.95	2.8	2.8

අනු අංකය	පාලනික කේතය	පාරම් නම	ආරම්භක බණ්ඩාංක (කාදවල ශ්‍රී ලංකා)		අවසාන බණ්ඩාංක (කාදවල ශ්‍රී ලංකා)		පාරම් දින (මිටර්)	පාරම් සාමාන්‍ය පළල (මිටර්)	සංවර්ධිත පළල (මිටර්)
			වම	දකුණ	වම	දකුණ			
63	SG/APS/B034/17	උඩුගල නවජනපදය මාර්ගය	157184.913/150645.936	157180.588/150644.712	157214.234/151039.016	157211.488/151036.106	537.82	4.0	3.0
64	SG/APS/B034/17/01	උඩුගල නවජනපදය මාර්ගයේ පළමු පටුම	157136.225/150717.328	157134.024/150715.029	157115.616/150802.37	157112.682/150802.997	126.93	3.0	3.0
65	SG/APS/B034/17/02	උඩුගල නවජනපදය මාර්ගයේ දෙවන පටුම	157194.701/150840.201	157193.513/150842.97	157238.397/150834.561	157258.816/150837.531	67.31	3.0	3.0
66	SG/APS/B034/17/03	උඩුගල නවජනපදය මාර්ගයේ තෙවන පටුම	157179.764/150851.724	157183.032/150849.121	157144.654/150802.344	157146.314/150798.704	64.78	4.0	3.0
67	SG/APS/B034/17/04	උඩුගල නවජනපදය මාර්ගයේ සිව්වන පටුම	157200.963/150891.536	157203.824/150894.019	157287.029/150857.015	157287.488/150859.98	97.11	3.0	3.0
68	SG/APS/B034/17/05	උඩුගල නවජනපදය මාර්ගයේ පස්වන පටුම	157216.086/150916.647	157213.762/150913.39	157127.214/150981.919	157125.388/150978.36	123.59	4.0	3.0
69	SG/APS/B034/18	අක්කර 20 මාර්ගය	156877.268/150804.353	156877.963/150800.9	156656.696/150684.219	156654.526/150679.967	304.82	3.5	3.0
70	SG/APS/B034/19	පරල තේ කර්මාන්තශාලා මාර්ගය	156572.965/151531.534	156566.092/151530.921	156786.029/151735.844	156782.224/151737.077	510.48	4.0	3.5
71	SG/APS/B034/20	මානකන්ද දළකැටිය පරලවත් මාර්ගය	156360.177/151676.944	156359.953/151672.728	155883.786/151411.51	155887.773/151411.84	611.81	4.0	2.6
72	SG/APS/B034/20/01	පරල කෝඩ්ලෝරවත් මාර්ගය	156168.376/151640.022	156171.544/151642.503	156236.059/151404.622	156238.258/151401.282	358.16	4.0	2.5
73	SG/APS/B034/20/02	පරල මානකන්ද මාර්ගය	156169.797/151646.132	156166.453/151643.627	155789.695/151426.375	155792.419/151429.304	593.3	4.0	2.5
74	SG/APS/B034/20/02/01	පරල කෙපෙල්කොටුව මාර්ගය	156157.289/151679.199	156154.634/151682.46	156034.065/151783.759	156034.102/151780.759	207.91	3.0	2.0
75	SG/APS/B034/20/02/02	පරල මානකන්ද මාර්ගයේ පළමු පටුම	156010.801/151671.013	156007.863/151670.303	155883.58/151868.857	155881.899/151871.343	342.96	3.0	2.4
76	SG/APS/B034/20/02/03	පරලකන්ද මාර්ගය	155843.954/151581.64	155840.732/151579.269	155314.994/151842.066	155311.916/151839.512	638.21	4.0	2.5
77	SG/APS/B034/20/02/04	මානකන්ද පරලකන්ද මාර්ගය	155772.657/151521.694	155771.718/151517.214	155589.382/151354.958	155591.602/151352.94	284.75	3.0	1.0
78	SG/APS/B034/21	පරල ගලවත්තන්ද නිරිඳල්ල මාර්ගය	156373.909/151711.103	156373.201/151716.646	156792.033/153926.13	156788.576/153926.675	2579.91	3.5	3.0

අනු අංකය	පාලනික කේතය	පාලන නම	ආරම්භක බණ්ඩාරක (කදවල ශ්‍රී ලංකා)		අවසාන බණ්ඩාරක (කදවල ශ්‍රී ලංකා)		පාලන දින (මිටර)	පාලන සාමාන්‍ය පළල (මිටර)	සංවර්ධන පළල (මිටර)
			වම	දකුණ	වම	දකුණ			
79	SG/APS/B034/21/01	කොඩිකාරපාලම මාර්ගය	156338.424/151964.35	156536.76/151960.071	156381.863/151983.084	156385.862/151982.999	214.84	4.0	2.5
80	SG/APS/B034/21/02	කිවිලිගේන කොඩිකාරපාලම මාර්ගය	156546.391/152043.263	156548.149/152048.114	156787.385/151893.95	156791.09/151895.46	310.94	4.0	3.0
81	SG/APS/B034/21/02/01	කිවිලිගේන කොඩිකාරපාලම මාර්ගයේ පළමු පටුම	156598.289/152032.348	156594.757/152034.194	156898.787/152008.165	156898.007/152011.062	321.58	3.0	2.0
82	SG/APS/B034/21/03	ගලපිටකන්ද පළමු පටුම	156571.617/152309.337	156570.741/152312.83	156623.027/152278.37	156626.563/152277.695	83.32	3.6	3.0
83	SG/APS/B034/21/04	ගලපිටකන්ද බතලවත්ත මාර්ගය	156573.555/152773.207	156574.564/152768.959	156404.175/152802.831	156402.073/152799.428	188.43	4.0	3.5
84	SG/APS/B034/21/05	පරලා ගලපිටකන්ද නිරිඳැල්ල අරඹි අඩි පාර	156607.192/152840.292	156608.18/152843.295	156645.905/152795.527	156648.802/152796.306	65.93	3.0	2.5
85	SG/APS/B034/22	පරලා අමුණේකන්ද මාර්ගය	156311.263/151852.193	156308.847/151853.986	156339.724/151947.712	156337.826/151949.633	114.43	2.7	2.5
86	SG/APS/B034/23	පරලා අමුණේකන්ද මාර්ගය	156018.482/152154.787	156015.62/152153.686	156165.389/152193.153	156167.56/152195.224	280.02	3.0	2.5
87	SG/APS/B034/24	පරලා පොකුණදෙස මාර්ගය	155906.959/152234.496	155903.953/152235.52	156005.52/152398.007	156004.741/152400.905	221.13	3.0	2.5
88	SG/APS/B034/25	පරලා කිරිඳිගේන මාර්ගය	155605.488/152254.823	155610.423/152254.601	155213.861/151898.401	155212.207/151895.898	756	3.0	2.6
89	SG/APS/B034/26	ඕනමල්වත්ත ගලපිටකන්ද මාර්ගය	155548.83/152342.896	155544.417/152344.581	156481.018/152489.773	156485.08/152492.253	1680	4.0	3.0
90	SG/APS/B034/26/01	ලෙඩ්කන්ද මාර්ගය පළමු පටුම	155812.259/152854.083	155807.217/152852.988	155881.989/152886.323	155882.927/152890.212	90.69	4.0	3.0
91	SG/APS/B034/26/02	ලෙඩ්කන්ද මාර්ගය දෙවන පටුම	156137.361/152707.502	156135.173/152709.799	156172.151/152815.675	156169.384/152814.517	151.73	3.0	3.0
92	SG/APS/B034/26/03	ලෙඩ්කන්ද මාර්ගය තෙවන පටුම	156141.391/152699.11	156145.003/152698.151	156061.22/152612.179	156064.117/152612.958	148.28	3.0	2.5
93	SG/APS/B034/27	ගුරුකඩ්දෙණ මාර්ගය	155206.007/152563.527	155204.082/152567.05	155242.19/152686.466	155238.344/152687.568	154.24	4.0	3.5
94	SG/APS/B034/28	පිල්ලවත්ත පළමු පටුම	154869.536/152691.801	154873.824/152690.24	154751.073/152596.152	154754.425/152598.333	221.14	4.0	3.5

අනු අංකය	පාලනික කේතය	පාරේ නම	ආරම්භක බේරුම්කරු (කැපවල ශ්‍රී ලංකා)		අවසාන බේරුම්කරු (කැපවල ශ්‍රී ලංකා)		පාරේ දිග (මීටර්)	පාරේ සාමාන්‍ය පළල (මීටර්)	සංවර්ධිත පළල (මීටර්)
			වම	දකුණ	වම	දකුණ			
95	SG/APS/B034/29	පහේ කඳුවල ඉහළ මාර්ගය	154809.16/152802.307	154805.185/152807.601	154907.573/152813.606	154908.043/152817.578	124.81	4.0	2.0
96	SG/APS/B034/30	පුස්සලකන්ද මාර්ගය	154427.166/153082.404	154420.883/153083.167	155488.137/152921.174	155487.906/152925.667	1275.64	4.5	4.0
97	SG/APS/B034/30/01	පුස්සලකන්ද අන්තර්ගත මාර්ගය	154792.381/153158.865	154787.287/153159.596	154753.1/153504.337	154749.634/153506.333	415.23	4.0	3.5
98	SG/APS/B034/30/01/01	පුස්සලකන්ද අන්තර්ගත මාර්ගයේ පළමු පටුම	154742.638/153222.09	154745.056/153218.001	154408.76/153347.892	154408.756/153343.891	374.39	4.0	3.5
99	SG/APS/B034/30/02	පුස්සලකන්ද ප්‍රජාගාරාම මාර්ගය	154998.718/153197	154993.134/153197.319	155037.456/153256.341	155035.567/153259.866	77.55	4.0	3.5
100	SG/APS/B034/30/03	පුස්සලකන්ද පළමු පටුම	155179.961/153156.997	155176.157/153158.242	155333.978/153314.694	155349.98/153314.623	304.23	4.0	3.5
101	SG/APS/B034/31	පිල්ලවත්ත මාර්ගය	154406.068/153077.414	154411.176/153077.68	154202.873/152646.25	154203.992/152642.41	520.81	4.0	3.0
102	SG/APS/B034/31/01	වැලිකොටුපොළ මාර්ගය	154338.58/152979.364	154338.638/152974.272	154245.307/153028.339	154245.823/153024.372	114.48	4.0	3.0
103	SG/APS/B034/31/02	පිල්ලවත්ත මාර්ගයේ පළමු පටුම	154350.511/152910.575	154352.063/152913.891	154496.07/152867.97	154498.125/152870.803	166.47	3.5	3.0
104	SG/APS/B034/31/03	පිල්ලවත්ත මාර්ගය	154304.71/152834.973	154305.897/152837.782	154522.292/152705.741	154521.95/152708.722	364.55	3.0	2.5
105	SG/APS/B034/31/03/01	පිල්ලවත්ත මාර්ගය	154388.387/152674.926	154392.563/152675.194	154550.972/152553.484	154548.342/152555.792	236.12	3.5	2.5
106	SG/APS/B034/31/04	පිල්ලවත්ත සිට ගෝණපැනිගල මාර්ගය	154275.162/152791.666	154274.09/152788.334	154205.965/152809.811	154206.026/152806.312	73.42	3.5	3.0
107	SG/APS/B034/32	පිඬුර ඉහළවත්ත අඩි පාර	154012.825/153424.749	154009.586/153424.804	154003.812/153644.448	154001.169/153645.868	246.52	3.0	2.0
108	SG/APS/B034/33	අම්බලන්වෙල මාර්ගය	153461.878/153590.973	153458.194/153589.411	153411.402/153660.025	153410.345/153656.167	116.18	4.0	3.5
109	SG/APS/B034/34	ගෝණපැනිගල මාර්ගය	153396.573/153201.848	153398.804/153204.009	154081.918/152867.054	154082.727/152869.943	817.68	3.0	2.5
110	SG/APS/B034/35	ගෝණපැනිගල මාර්ගයේ පළමු කොටස	153389.272/152995.541	153393.184/152998.685	153341.616/152602.786	153341.848/152598.292	482.11	4.5	4.0

අනු අංකය	පාලනික කේතය	පාරේ නම	ආරම්භක බණ්ඩාරක (කදවල ශ්‍රී ලංකා)		අවසාන බණ්ඩාරක (කදවල ශ්‍රී ලංකා)		පාරේ දිග (මීටර්)	පාරේ සාමාන්‍ය පළල (මීටර්)	සංවර්ධිත පළල (මීටර්)
			වම	දකුණ	වම	දකුණ			
111	SG/APS/B034/35/01	මානකන්ද මාර්ගය	153430.222/152736.929	153435.079/152739.957	154342.32/152408.172	154342.144/152412.168	1190.05	4.0	3.5
112	SG/APS/B034/35/01/01	මානකන්ද මාර්ගයේ පළමු පටුම	153899.665/152576.357	153895.645/152579.514	153984.239/152618.235	153981.568/152620.496	101.89	3.5	3.0
113	SG/APS/B034/35/01/02	මානකන්ද මාර්ගයේ දෙවන පටුම	154039.118/152485.79	154036.953/152488.545	154106.259/152595.084	154104.673/152598.204	134.09	3.5	3.0
114	SG/APS/B034/35/01/03	මානකන්ද මාර්ගයේ තෙවන පටුම	154041.481/152462.55	154041.738/152459.016	153662.298/152526.853	153659.966/152524.243	405.75	3.5	3.0
115	SG/APS/B034/35/01/04	මානකන්ද මාර්ගයේ සිව්වන පටුම	154126.013/152332.949	154130.983/152333.176	154153.784/152303.817	154154.445/152307.255	48.53	3.5	3.0
116	SG/APS/B034/35/02	කුඹුරුපේන මාර්ගය	153368.378/152619.278	153372.246/152625.574	153339.415/151563.978	153342.627/151565.367	1204.47	3.5	3.0
117	SG/APS/B034/36	කිඳිලපේන මාර්ගය	153305.628/153129.141	153306.867/153125.338	153206.548/152910.147	153210.448/152911.03	285.42	4.0	3.0
118	SG/APS/B034/37	කදවැල්දොළ මාර්ගය	153249.311/153215.57	153252.33/153213.785	152981.28/152948.11	152983.391/152943.015	423.1	3.5	3.0
119	SG/APS/B034/38	හමේ කඹුට සිට කදවැල්දොළ මාර්ගය	153053.703/153278.299	153056.199/153276.109	152948.854/152799.077	152951.034/152796.734	1122	3.2	3.0
120	SG/APS/B034/38/01	වැඩවුන්පේන මාර්ගය	152713.194/153309.444	152711.435/153304.691	152375.237/153406.448	152373.893/153403.216	366.85	3.5	3.0
121	SG/APS/B034/38/02	ටකරන්වත්ත මාර්ගය	152680.037/153166.182	152682.453/153163.284	152597.369/153144.862	152598.195/153141.461	94.28	3.5	3.0
122	SG/APS/B034/39	ඇල්ලකොඩි සිට පිඹුර මාර්ගය	153159.174/153546.815	153157.519/153553.13	153482.772/153802.755	153479.861/153807.714	613.27	4.0	3.6
123	SG/APS/B034/40	ඇලුත්තෙවත්ත මාර්ගය	153010.665/153748.025	153009.109/153751.891	153219.447/153770.356	153216.519/153773.082	268.12	4.0	4.0
124	SG/APS/B034/41	එගොඩවත්ත මාර්ගය	152952.76/153792.175	152954.849/153789.182	152590.784/154044.446	152595.397/154047.95	764.66	3.5	3.0
125	SG/APS/B034/42	එඩිට්වත්ත මාර්ගය	152873.971/153877.869	152877.218/153875.483	152835.639/153831.498	152838.333/153828.542	65.1	4.0	3.7
126	SG/APS/B034/43	නිකගොඩ උඩවත්ත මාර්ගය	152657.431/154083.67	152654.879/154083.362	152360.208/154587.182	152360.132/154584.673	713.87	2.5	2.0

අනු අංකය	පාලනික කේතය	පාරම්පරික නම	ආරම්භක බණ්ඩාංක (කාදවල ශ්‍රී ලංකා)		අවසාන බණ්ඩාංක (කාදවල ශ්‍රී ලංකා)		පාරම්පරික දින (මිටර්)	පාරම්පරික පළල (මිටර්)	සංවර්ධිත පළල (මිටර්)
			වම	දකුණ	වම	දකුණ			
127	SG/APS/B034/44	නිකගොඩ උඩුකුඹුර පළමු මාර්ගය	152348.275/154207.188	152352.569/154205.401	152199.322/154093.296	152202.807/154092.968	227.71	3.5	2.8
128	SG/APS/B034/45	නිකගොඩ අළුතේ මාර්ගය	152293.939/154277.524	152292.666/154282.208	151888.105/155763.132	151885.466/155765.432	1893.83	3.5	3.0
129	SG/APS/B034/45/01	අළුතේ මාර්ගය	152356.698/154587.11	152356.433/154583.337	152159.211/154687.009	152157.809/154683.802	265.83	3.5	3.0
130	SG/APS/B034/45/02	නිකගොඩ අළුතේ මාර්ගය	151857.452/155248.606	151858.086/155245.608	151465.03/155520.798	151466.274/155518.069	539.24	3.0	3.0
131	SG/APS/B034/45/03	නිකගොඩ අළුතේ මාර්ගය	151863.251/155311.934	151863.102/155316.035	152001.775/155288.691	152004.081/155291.959	155.73	4.0	3.5
132	SG/APS/B034/45/04	නිකගොඩ අළුතේ මාර්ගය	151801.975/155463.935	151800.363/155460.522	151732.14/155523.606	151729.672/155521.122	101.62	3.5	3.0
133	SG/APS/B034/45/05	නිකගොඩ අළුතේ මාර්ගය	151836.428/155524.305	151834.142/155521.646	151834.407/155586.377	151835.461/155589.714	117.35	3.5	3.0
134	SG/APS/B034/46	නිකගොඩ උඩුකුඹුර දෙවන මාර්ගය	152258.501/154304.292	152263.252/154301.889	152204.333/154227.006	152207.714/154227.914	141.05	3.5	3.0
135	SG/APS/B034/47	නිකගොඩ උඩුකුඹුර තෙවන මාර්ගය	152069.276/154356.638	152072.633/154356.714	152142.219/154268.253	152144.721/154269.909	121.34	3.0	2.6
136	SG/APS/B034/48	නිකගොඩ පළමු පවුම	151954.285/154343.495	151957.929/154340.37	151929.476/154249.566	151930.281/154252.456	221.65	3.0	2.5
137	SG/APS/B034/49	අක්කර 08 ඇල්ලකඩේවත්ත මාර්ගය	151611.061/154472.237	151614.777/154471.403	151773.68/154023.63	151774.069/154020.655	760.82	3.0	3.0
138	SG/APS/B034/49/01	අක්කර 05 ඉඹුලහිටිපේන මාර්ගය	151938.098/154056.691	151941.446/154057.97	151932.947/153924.582	151934.081/153921.271	182.92	3.5	3.0
139	SG/APS/B034/50	නිකගොඩ ගොඩපොළ මාර්ගය	151211.374/154544.621	151203.484/154546.446	151235.423/154749.043	151236.685/154745.247	436.11	4.0	3.5
140	SG/APS/B034/51	හල්ගහපේන මාර්ගය	150926.637/154660.74	150923.79/154661.863	151152.756/154757.59	151154.921/154759.668	334.47	3.0	2.8
141	SG/APS/B034/52	හැඬුවත්ත මාර්ගය	150683.495/154788.477	150679.725/154789.884	150827.894/155031.371	150830.496/155033.973	730.23	3.7	3.0
142	SG/APS/B034/52/01	හැඬුවත්ත මාර්ගයේ පළමු පවුම	150621.161/155143.169	150617.249/155142.86	150647.233/155275.072	150643.57/155274.726	137.17	3.7	3.0

අනු අංකය	පාලනික කේතය	පාරේ නම	ආරම්භක බණ්ඩාරක (කැවල ශ්‍රී ලංකා)		අවසාන බණ්ඩාරක (කැවල ශ්‍රී ලංකා)		පාරේ දිග (මීටර්)	පාරේ සාමාන්‍ය පළල (මීටර්)	සංවර්ධිත පළල (මීටර්)
			වම	දකුණ	වම	දකුණ			
143	SG/APS/B034/52/02	හැබ්බාලේ මාර්ගයේ දෙවන පටුම	150789.859/155060.569	150786.209/155063.43	150892.89/155196.562	150889.895/155198.701	193.95	3.7	3.0
144	SG/APS/B034/53	සේනායා මාර්ගයේ දෙවන කොටස	150599.829/154744.569	150604.025/154746.216	151605.162/153221.781	151608.029/153225.251	2437.92	4.5	4.0
145	SG/APS/B034/53/01	සේනායා මාර්ගයේ දෙවන කොටසේ පළමු පටුම	150901.005/154361.832	150897.724/154364.184	150941.086/154398.682	150937.589/154400.624	56.74	4.0	3.7
146	SG/APS/B034/53/02	සේනායා මාර්ගයේ දෙවන කොටසේ දෙවන පටුම	150915.379/154325.617	150916.725/154321.271	150779.801/154122.92	150783.759/154123.499	277.12	4.0	3.5
147	SG/APS/B034/53/03	සේනායා මාර්ගයේ දෙවන කොටසේ තෙවන පටුම	150956.967/154236.316	150955.374/154240.109	151083.371/154306.853	151079.378/154307.09	151.05	4.0	3.5
148	SG/APS/B034/53/04	පොල්වත්ත කඳුගලසේනායා මාර්ගය	151280.724/153714.697	151277.754/153717.657	151723.026/153871.479	151724.304/153875.269	889.95	4.0	3.6
149	SG/APS/B034/53/05	පොල්වත්ත කොස්ගලසේන මාර්ගය	151285.14/153710.987	151281.635/153713.771	151446.688/153665.393	151450.429/153666.811	209.62	4.0	3.7
150	SG/APS/B034/53/06	පොල්වත්ත මිරිස්සේන මාර්ගය	151566.103/153465.149	151565.211/153468.661	152196.977/153652.594	152193.511/153653.566	760.52	3.6	3.2
151	SG/APS/B034/53/06/01	පොල්වත්ත මිරිස්සේන මාර්ගයේ පළමු පටුම	151726.981/153602.314	151729.907/153603.013	151852.779/153438.163	151852.292/153441.124	250.01	3.0	3.0
152	SG/APS/B034/53/06/02	පොල්වත්ත මිරිස්සේන මාර්ගයේ දෙවන පටුම	151938.141/153656.04	151942.147/153656.042	151937.134/153620.166	151939.911/153623.044	37.22	4.0	3.5
153	SG/APS/B034/53/06/03	පොල්වත්ත මිරිස්සේන මාර්ගයේ තෙවන පටුම	151953.98/153659.429	151958.172/153663.244	151999.971/153630.358	152002.072/153633.762	59.18	4.0	3.5
154	SG/APS/B034/53/06/04	පොල්වත්ත මිරිස්සේන මාර්ගයේ සිව්වන පටුම	152047.02/153658.921	152043.299/153660.465	152055.735/153689.167	152052.301/153687.115	37.6	4.0	3.7
155	SG/APS/B034/53/07	පොල්වත්ත පන්සල මාර්ගය	151594.161/153234.354	151588.103/153236.539	151564.82/153306.85	151560.827/153306.625	112.84	4.0	3.5
156	SG/APS/B034/C404/01	ඇල්ලමඩ් මාර්ගය	160232.449/148423.492	160234.269/148419.848	160102.703/148258.795	160106.689/148259.126	274.56	4.0	3.5
157	SG/APS/B034/C404/02	අයගම ප්‍රාදේශීය සභාව අසල මාර්ගය	160277.687/148300.551	160275.962/148303.6	160360.472/148318.25	160361.682/148321.535	100.54	3.5	2.5

අනු අංකය	පාලනික කේතය	පාරේ නම	ආරම්භක බේරුම්කරු (කැපවල ශ්‍රී ලංකා)		අවසාන බේරුම්කරු (කැපවල ශ්‍රී ලංකා)		පාරේ දිග (මීටර්)	පාරේ සාමාන්‍ය පළල (මීටර්)	සංවර්ධිත පළල (මීටර්)
			වම	දකුණ	වම	දකුණ			
158	SG/APS/B034/C404/03	අයගම ගල් පන්තල මාර්ගය	160514.894/147862.732	160512.387/147864.916	161099.332/148315.776	161100.116/148318.981	1238.54	3.3	3.3
159	SG/APS/B034/C404/04	අයගම තේණපලවත්ත මාර්ගය	160664.062/147685.186	160661.14/147687.992	160692.86/147811.045	160690.171/147809.713	165.78	3.0	3.0
160	SG/APS/B034/C404/05	යකච්ඡවෙල චිත්තැන්න මාර්ගය	160703.313/147661.927	160707.299/147661.312	160874.516/146570.34	160876.68/146573.853	1755.09	4.0	3.5
161	SG/APS/B034/C404/05/01	විවෙර්ට මාර්ගය	160882.102/146903.71	160881.546/146904.545	160919.215/146948.385	160918.248/146948.684	62.65	1.0	1.0
162	SG/APS/B034/C404/05/02	යකච්ඡවෙල චිත්තැන්න ඒ කොටස මාර්ගයේ පළමු පටුම	160737.493/146781.269	160742.01/146768.491	160483.043/146788.777	160479.708/146786.569	313.38	4.0	3.5
163	SG/APS/B034/C404/06	අමුණුබුර්ට මාර්ගය	161113.758/147357.258	161115.071/147355.093	160997.494/147284.759	160999.217/147282.947	172.08	2.5	2.0
164	SG/APS/B034/C404/07	පල්ලෙකඩ පියන්තෙවත්ත මාර්ගය	161319.55/147244.647	161317.94/147247.179	161595.737/147295.555	161595.182/147298.504	334.92	3.0	3.0
165	SG/APS/B034/C404/08	පල්ලෙකඩ කලවුකන්ද මාර්ගය	161589.331/146890.54	161590.577/146893.912	163580.055/146010.311	163581.573/146013.464	2723.02	3.5	3.0
166	SG/APS/B034/C404/08/01	පල්ලෙකඩ කලවුකන්ද මාර්ගයේ පළමු පටුම	161765.24/146834.981	161762.385/146837.761	162260.645/146827.904	162261.944/146831.153	592.87	3.5	3.0
167	SG/APS/B034/C404/08/01/01	පල්ලෙකඩ කලවුකන්ද මාර්ගයේ පළමු පටුමෙහි පළමු අතුරු මාර්ගය	161877.614/146942.89	161874.052/146943.326	161836.74/147058.352	161834.092/147056.064	130.08	3.5	3.0
168	SG/APS/B034/C404/08/01/02	පල්ලෙකඩ කලවුකන්ද මාර්ගයේ පළමු පටුමෙහි දෙවන අතුරු මාර්ගය	162068.884/146903.431	162064.528/146903.699	162065.967/147192.316	162063.483/147189.851	363.6	3.5	3.0
169	SG/APS/B034/C404/08/02	පල්ලෙකඩ කලවුකන්ද මාර්ගයේ දෙවන පටුම	162095.484/146610.42	162092.231/146612.057	162075.851/146720.112	162072.543/146718.972	159.95	3.5	3.0
170	SG/APS/B034/C404/08/03	පල්ලෙකඩ කලවුකන්ද මාර්ගයේ තෙවන පටුම	162235.225/146567.227	162231.787/146568.616	162277.016/146608.193	162274.259/146609.377	67.91	3.0	2.5
171	SG/APS/B034/C404/08/04	පල්ලෙකඩ කලවුකන්ද මාර්ගයේ සිව්වන පටුම	162330.51/146539.017	162327.516/146539.222	162327.146/146639.195	162324.43/146637.919	119.75	3.0	2.5

අනු අංකය	පාලනික කේතය	පාලන නම	ආරම්භක බණ්ඩාරක (කදවල ශ්‍රී ලංකා)		අවසාන බණ්ඩාරක (කදවල ශ්‍රී ලංකා)		පාලන දින (මිටර)	පාලන සාමාන්‍ය පළල (මිටර)	සංවර්ධිත පළල (මිටර)
			වම	දකුණ	වම	දකුණ			
172	SG/APS/B034/C404/08/05	පල්ලකෙඩ කලවුකන්ද මාර්ගයේ පස්වන පවුම	162878.678/146452.22	162879.894/146456.27	162965.425/146459.726	162966.543/146463.043	113.09	3.5	3.0
173	SG/APS/B034/C404/08/06	පල්ලකෙඩ කලවුකන්ද මාර්ගයේ සයවන පවුම	163249.055/146310.42	163251.852/146306.72	163186.802/146249.491	163185.128/146245.858	101.44	4.0	3.5
174	SG/APS/B034/C404/08/07	පල්ලකෙඩ කලවුකන්ද මාර්ගයේ හත්වන පවුම	163349.292/146179.163	163350.69/146182.28	163466.236/146261.559	163469.087/146263.589	210.97	3.5	3.0
175	SG/APS/B034/C404/09	පල්ලකෙඩ විවේචිට මාර්ගය	161542.933/146841.653	161545.476/146844.786	160870.378/146980.519	160869.878/146976.55	762.46	4.0	3.0
176	SG/APS/B034/C404/09/01	විවේචිට බටවල දේවාල මාර්ගය	161530.816/146859.802	161526.513/146860.001	161513.995/146908.75	161510.7/146906.482	54.77	4.0	3.0
177	SG/APS/B034/C404/09/02	පල්ලකෙඩ විවේචිට මාර්ගයේ පළමු පවුම	161244.901/146852.016	161247.853/146851.472	161170.512/146835.73	161171.291/146832.833	88.88	3.0	3.0
178	SG/APS/B034/C404/10	පල්ලකෙඩ කපුගෙවත්ත පළමු මාර්ගය	161473.741/146680.398	161471.855/146677.447	161178.081/146730.885	161181.339/146729.607	331.29	3.5	3.0
179	SG/APS/B034/C404/11	පල්ලකෙඩ කපුගෙවත්ත දෙවන මාර්ගය	161465.864/146666.822	161464.162/146663.758	161370.433/146707.203	161370.628/146703.708	112.86	3.5	3.0
180	SG/APS/B034/C404/12	පල්ලකෙඩ කපුගෙවත්ත තෙවන මාර්ගය	161319.608/146495.3	161318.655/146491.334	161145.813/146562.262	161144.251/146558.58	192.67	4.0	3.5
181	SG/APS/B034/C404/13	බෝගහවාගුව අතුරු මාර්ගය	160804.117/146384.218	160801.495/146382.584	160452.028/146512.394	160453.507/146509.784	418.81	3.0	3.0
182	SG/APS/B034/C404/13/01	බෝගහවෙල පළමු පවුම	160714.613/146378.184	160717.357/146376.873	160680.716/146305.937	160683.448/146304.696	81.59	3.0	3.0
183	SG/APS/B034/C404/13/02	බෝගහවෙල දෙවන පවුම	160663.341/146420.705	160665.793/146418.821	160614.46/146365.428	160615.045/146362.485	80.35	3.0	3.0
184	SG/APS/B034/C404/14	පිටකන්ද මිදුළිකන්ද මාර්ගය	160597.821/145684.591	160599.598/145687.607	160793.718/145549.191	160795.465/145552.225	245.86	3.5	2.7
185	SG/APS/B034/C404/15	පිටකන්ද මල්ගහගේ මාර්ගය	160800.708/145218.773	160803.44/145216.441	160467.232/143887.714	160470.507/143889.052	1695.47	3.5	2.5
186	SG/APS/B034/C404/15/01	පිටකන්ද මල්ගහගේ පළමු පවුම	160667.954/144809.794	160667.565/144806.819	160250.128/145116.823	160248.197/145114.528	554.23	3.0	3.0

අනු අංකය	පාලනික කේතය	පාරම්පරික නම	ආරම්භක බණ්ඩාංක (කැවල ශ්‍රී ලංකා)		අවසාන බණ්ඩාංක (කැවල ශ්‍රී ලංකා)		පාරම්පරික දින (මිටර්)	පාරම්පරික සාමාන්‍ය පළල (මිටර්)	සංවර්ධිත පළල (මිටර්)
			වම	දකුණ	වම	දකුණ			
187	SG/APS/B034/C404/16	ගවරිගිරිය පළමු පවුම	161128.747/144589.87	161128.216/144586.652	161049.572/144682.218	161046.572/144682.209	147.67	3.0	3.0
188	SG/APS/B034/C404/17	ගවරිගිරිය දෙවන පවුම	161135.292/144579.446	161135.64/144582.433	161180.913/144512.54	161182.41/144515.14	130.99	3.0	3.0
189	SG/APS/B034/C404/18	ගවරිගිරිය තෙවන පවුම	161127.88/144464.7	161127.449/144461.227	161062.547/144493.465	161062.922/144489.985	77.67	3.5	3.0
190	SG/APS/B034/C404/19	ගවරිගිරිය රයිමම්කන්ද දුම්බරමානාන මාර්ගය	161779.411/143034.835	161779.803/143040.087	164105.157/141682.101	164098.104/141693.573	2827.95	5.0	2.8
191	SG/APS/B034/C404/19/01	රයිමම්කන්ද පළමු පවුම	162472.51/142538.194	162477.055/142538.346	162926.879/142179.351	162924.239/142181.648	598.79	3.5	2.5
192	SG/APS/B034/C404/20	චතුකාරගම පුවත්ත මාර්ගය	161830.697/142377.098	161831.329/142372.877	161658.235/142284.563	161660.779/142281.477	200.13	4.0	2.5
193	SG/APS/B034/C404/20/01	චතුකාරගම ගල්වත්ත මාර්ගය	161770.912/142351.185	161767.49/142348.967	161407.504/142626.852	161406.567/142622.963	484.68	4.0	2.5
194	SG/APS/B034/C404/21	චතුකාරගම ඇඟිලිකන්ත මාර්ගය	161854.188/142336.153	161857.671/142334.179	162065.157/142085.338	162069.155/142085.488	465.95	4.0	2.5
195	SG/APS/B034/C404/21/01	චතුකාරගම ඇඟිලිකන්ත මාර්ගයේ පළමු පවුම	161853.994/142265.949	161857.565/142259.677	161772.003/142238.716	161770.111/142236.387	210.73	3.0	2.5
196	SG/APS/B034/C404/22	චතුකාරගම දොරලඞ්චිය මාර්ගය	162332.269/142015.546	162336.192/142013.515	162224.993/141974.511	162227.987/141971.858	124.22	4.0	3.0
197	SG/APS/B034/C404/D405/01	පල්ලෙකඩ වැලිකඩවත්ත මාර්ගය	161844.513/146592.528	161847.643/146590.71	161750.31/146468.354	161753.01/146467.049	233.54	3.0	2.0
198	SG/APS/B034/C404/D405/02	පල්ලෙකඩ ගම්කන්ද පළමු පවුම	162037.316/146402.471	162040.726/146400.334	162174.399/145975.895	162175.937/145979.587	563.2	4.0	2.7
199	SG/APS/B034/C404/D405/03	පල්ලෙකඩ ගම්කන්ද දෙවන පවුම	162453.292/146174.872	162456.176/146173.464	162428.868/145826.889	162431.61/145825.195	399.09	3.0	2.5
200	SG/APS/B034/C404/D405/04	පල්ලෙකඩ කලුවකන්ද පළමු පවුම	162474.041/146170.034	162470.718/146171.919	162504.53/146482.959	162500.934/146484.458	488.03	3.8	3.0
201	SG/APS/B034/C404/D405/05	පල්ලෙකඩ කලුවකන්ද දෙවන පවුම අඩ්ඩාර	162686.261/146095.816	162683.748/146096.055	162811.398/146422.064	162808.898/146422.148	478.88	2.5	1.0

අනු අංකය	පාලනික කේතය	පාලන නම	ආරම්භක බණ්ඩාංක (කෙටි ලංකා)		අවසාන බණ්ඩාංක (කෙටි ලංකා)		පාලන දින (මිටර්)	පාලන සාමාන්‍ය පළල (මිටර්)	සංවර්ධන පළල (මිටර්)
			වම	දකුණ	වම	දකුණ			
202	SG/APS/B034/C404/D405/06	ගංගොඩකන්ද මැල්ගොඩැල්ල මාර්ගය	162968.06/145953.49	162965.454/145954.98	163006.478/146187.935	163003.508/146188.359	262.04	3.0	2.6
203	SG/APS/B034/C404/D405/07	ගංගොඩකන්ද අක්කර 60 කලවුකන්ද මාර්ගය	163512.077/145858.981	163508.787/145861.253	163471.577/146000.074	163469.503/145995.972	176.79	3.0	2.0
204	SG/APS/B034/C404/D405/08	වටකුරුගල මාර්ගය	163588.386/145811.609	163591.924/145808.958	164489.39/144732.269	164490.466/144736.122	1968.75	4.0	3.3
205	SG/APS/B034/C404/D405/08/01	වටකුරුගල භේත්තයාය මාර්ගය	163566.841/145755.912	163568.726/145759.463	163965.736/145418.686	163968.755/145414.624	645.72	4.0	3.5
206	SG/APS/B034/C404/D405/08/02	ඇල්ලිට් භේත්තයාය මාර්ගය	163496.965/145572.992	163499.761/145569.916	163253.998/145287.284	163257.699/145288.802	628.02	4.0	3.5
207	SG/APS/B034/C404/D405/08/03	කැටකැරැල්ල භේත්තයාය මාර්ගය	163616.035/145268.563	163613.876/145271.966	164357.348/145066.841	164354.49/145069.726	961.49	4.0	3.5
208	SG/APS/B034/C404/D405/09	භේත්තයාය කැටකැරැල්ල පහළ මාර්ගය	163990.074/145237.543	163987.423/145240.036	163851.196/145487.983	163851.066/145484.486	364.15	3.5	2.5
209	SG/APS/B034/C404/D405/09	අක්කර 36 පළමු පවුම	163800.119/145712.003	163797.125/145714.771	164706.8/145736.521	164709.94/145738.999	1311.94	4.0	3.5
210	SG/APS/B034/C404/D405/10	අක්කර 36 දෙවන පවුම	164021.24/145639.8	164017.23/145641.462	163951.793/145849.01	163947.772/145849.286	415.39	4.0	3.5
211	SG/APS/B034/C404/D405/11	බදවෙලකන්ද ගල්කැරැකන්ද මාර්ගය	165014.641/145280.167	165015.231/145284.137	165346.832/145401.242	165346.488/145405.227	431.27	4.0	3.5
212	SG/APS/B034/C404/D405/11/01	ගල්කැරැකන්ද ගලකුර මාර්ගය	165158.3/145353.973	165152.821/145351.331	166198.582/145939.273	166195.509/145937.524	1493.54	3.0	2.5
213	SG/APS/B034/C404/D405/12	බදවෙලකන්ද අක්කර 100 අතුරු මාර්ගය	165015.18/145244.641	165017.981/145242.209	165068.311/145044.802	165069.977/145046.032	223.49	2.0	1.0
214	SG/APS/B034/C404/D408/01	ලඹුඇලභේත මාර්ගය	160521.458/145830.534	160525.82/145828.924	160432.723/145663.672	160436.722/145663.788	281.21	4.0	3.5
215	SG/APS/B034/C404/D408/02	තේ ජනපදය මහින්දාගමය මාර්ගය	160446.711/145882.744	160442.926/145885.192	160619.012/146203.898	160615.756/146202.615	457.76	3.5	3.0
216	SG/APS/B034/C404/D408/02/01	තේ ජනපදය මහින්දාගමය මාර්ගයේ පළමු පවුම	160442.851/145922.735	160442.156/145926.425	160483.797/145913.543	160481.311/145916.511	47.94	3.5	3.0

අනු අංකය	පාලනික කේතය	පාරේ නම	ආරම්භක බණ්ඩාංක (කදවල ශ්‍රී ලංකා)		අවසාන බණ්ඩාංක (කදවල ශ්‍රී ලංකා)		පාරේ දිග (මීටර්)	පාරේ සාමාන්‍ය පළල (මීටර්)	සංවර්ධිත පළල (මීටර්)
			වම	දකුණ	වම	දකුණ			
217	SG/APS/B034/C404/D408/02/02	නේ ජනපදය මහින්දාරාමය මාර්ගයේ දෙවන පවුම	160436.421/145971.767	160435.934/145975.38	160544.63/145900.79	160546.658/145903.644	169.64	3.5	3.0
218	SG/APS/B034/C404/D408/02/02/01	නේ ජනපදය මහින්දාරාමය මාර්ගයේ දෙවන පවුමගෙහි පළමු අතුරු මාර්ගය	160483.556/145920.016	160481.336/145924.6	160511.205/145979.264	160508.558/145977.853	77.25	3.0	2.0
219	SG/APS/B034/C404/D408/02/03	නේ ජනපදය මහින්දාරාමය මාර්ගයේ තෙවන පවුම	160497.179/146104.457	160502.297/146106.814	160622.966/146038.814	160623.854/146042.199	157.01	3.5	3.0
220	SG/APS/B034/C404/D408/02/04	නේ ජනපදය මහින්දාරාමය මාර්ගයේ සිව්වන පවුම	160613.368/146186.927	160617.507/146187.826	160787.105/146149.908	160786.575/146153.368	189.6	3.5	3.0
221	SG/APS/B034/C404/D408/03	මහින්දාරාමය පළමු පවුම	160355.127/146027.079	160352.312/146029.781	160402.833/146058.487	160403.62/146061.383	77.36	3.0	3.0
222	SG/APS/B034/C404/D408/04	හේමානැට සමඟි මාවත	160333.715/146026.165	160330.912/146023.308	159539.665/146365.582	159545.419/146358.971	1699.38	4.0	3.0
223	SG/APS/B034/C404/D408/04/01	හේමානැට සමඟි මාවතෙහි පළමු පවුම	159844.226/146691.312	159841.171/146691.491	160035.912/146800.095	160032.973/146800.693	280.25	3.0	2.5
224	SG/APS/B034/C404/D408/04/01/01	හේමානැට සමඟි මාවතෙහි පළමු පවුමගෙහි පළමු අතුරු මාර්ගය	159861.741/146731.182	159857.518/146729.35	159889.727/146770.212	159887.787/146770.695	54.14	2.0	2.0
225	SG/APS/B034/C404/D408/04/02	හේමානැට සමඟි මාවතෙහි දෙවන පවුම	159728.552/146728.858	159724.349/146728.619	159621.929/146975.422	159618.476/146973.403	477.04	4.0	3.0
226	SG/APS/B034/C404/D408/04/02/01	හේමානැට සමඟි මාවතෙහි දෙවන පවුමගෙහි පළමු අතුරු මාර්ගය -අඩ්පාර	159684.662/146936.945	159685.741/146936.62	159659.818/146854.201	159660.429/146853.41	114.3	1.0	1.0
227	SG/APS/B034/C404/D408/04/03	තයදැගල පන්සල මාර්ගය	159527.537/146619.396	159528.152/146616.423	159454.032/146835.225	159452.04/146837.468	272.6	3.0	3.0
228	SG/APS/B034/C404/D408/05	නේ ජනපදය මානෙල් මාවත	160127.361/145996.403	160136.435/145993.731	159972.445/145325.07	159976.308/145326.109	1066.31	4.0	3.0
229	SG/APS/B034/C404/D408/06	පිටකන්ද නේ ජනපදය මාර්ගයේ පළමු පවුම	159935.545/146138.611	159931.765/146137.118	160021.294/146332.061	160017.931/146334.367	237.03	4.0	3.0
230	SG/APS/B034/C404/D408/07	පිටකන්ද නේ ජනපදය මාර්ගයේ දෙවන පවුම	159904.209/146054.641	159908.641/146056.417	159969.111/146013.315	159972.1/146015.971	80.33	4.0	3.0

අනු අංකය	පාලනික කේතය	පාරේ නම	ආරම්භක බණ්ඩාරක (කදවල ශ්‍රී ලංකා)		අවසාන බණ්ඩාරක (කදවල ශ්‍රී ලංකා)		පාරේ දිග (මීටර්)	පාරේ සාමාන්‍ය පළල (මීටර්)	සංවර්ධිත පළල (මීටර්)
			වම	දකුණ	වම	දකුණ			
231	SG/APS/B034/C404/D408/08	පේරාගමුවේ ඇතුළු මාර්ගය	159857.111/146242.784	159853.795/146244.029	159711.282/146499.991	159709.728/146496.855	358.11	3.5	2.5
232	SG/APS/B034/C404/D408/09	තේ ජනපදය දිවුල්පොත්ත මාර්ගය	159460.488/146382.954	159464.417/146384.485	159785.131/145677.525	159788.05/145679.456	987.55	3.5	2.5
233	SG/APS/B034/C404/D408/10	තේ ජනපදය බටහේන මාර්ගය	159381.228/146257.082	159383.543/146259.709	158653.716/145864.021	158653.703/145860.52	1088	3.5	2.5
234	SG/APS/B034/C404/D408/10/01	තේ ජනපදය බටහේන මාර්ගයේ පළමු පටුම	159023.381/145826.412	159026.802/145825.655	159031.943/145705.343	159035.056/145703.743	128.99	3.5	2.5
235	SG/APS/B034/C404/D408/10/02	බටහේන ගඟබඩතැන්න මාර්ගය	158823.117/145833.604	158827.38/145833.628	157898.987/146369.526	157897.891/146365.679	1281.97	4.0	2.5
236	SG/APS/B034/C404/D408/10/03	බටහේන ගඟබඩතැන්න මාර්ගයේ පළමු පටුම	158123.941/146033.877	158126.979/146032.992	158118.056/145966	158120.711/145967.398	71.9	3.0	2.5
237	SG/APS/B034/C404/D408/10/03	බටහේන පන්විලතැන්න මාර්ගය	158665.833/145861.996	158662.019/145863.469	158452.434/146279.232	158454.773/146275.988	640.35	4.0	3.0
238	SG/APS/B034/C404/D408/11	තේ ජනපදය නාමණ්ඩිය මාර්ගය	159260.484/146291.527	159260.331/146287.138	159027.237/146166.165	159026.768/146162.697	348.73	3.5	2.5
239	SG/APS/B034/C404/D408/12	කදුගුලින්දොළ ගලපල්ල මාර්ගය	159290.047/146758.405	159287.228/146760.688	160057.767/147501.851	160054.738/147503.62	1411.76	3.5	2.5
240	SG/APS/B034/C404/D408/13	පිටකන්ද කෙඹුල්පොත්ත ගම්පහා මාර්ගය	158992.757/146918.043	158988.008/146924.988	159832.598/147571.895	159828.886/147573.398	1487.5	4.0	2.0
241	SG/APS/B034/C404/D408/14	පිටකන්ද කලපත්තල ගඟ මාර්ගය	158955.393/146975.354	158951.401/146974.973	156821.817/149321.023	156824.14/149317.398	4026.87	4.0	2.8
242	SG/APS/B034/C404/D408/14/01	පිටකන්ද කලපත්තල මාර්ගය	158841.061/147045.431	158837.28/147049.861	158171.437/147818.672	158172.122/147814.73	1444.73	4.0	2.5
243	SG/APS/B034/C404/D408/14/02	පිටකන්ද කලපත්තල මාර්ගයේ පළමු පටුම	157498.96/147878.859	157499.586/147874.677	157234.824/148089.31	157231.423/148087.205	361.03	4.0	2.5
244	SG/APS/B034/C404/D408/15	පිටකන්ද පළමු පටුම - අභිපාර	158952.29/146786.431	158950.896/146783.128	158653.804/146783.737	158655.668/146779.791	330.99	3.0	2.6
245	SG/APS/B034/C404/D408/16	පිටකන්ද පන්විලතැන්න මාර්ගය	158992.752/146695.263	158995.733/146698.178	158585.268/146197.093	158584.856/146193.067	839.02	4.0	3.0

අනු අංකය	පාලනික කේතය	පාරම්පරික නම	ආරම්භක බණ්ඩාංක (කාදවල ශ්‍රී ලංකා)		අවසාන බණ්ඩාංක (කාදවල ශ්‍රී ලංකා)		පාරම්පරික දින (මිටර්)	පාරම්පරික පළල (මිටර්)	සංවර්ධිත පළල (මිටර්)
			වම	දකුණ	වම	දකුණ			
246	SG/APS/B034/C404/D408/17	පිටකන්ද මාර්ගයේ දෙවන පටුම	158938.103/146697.138	158942.203/146696.806	158961.325/146672.98	158964.134/146674.035	36.88	3.0	2.6
247	SG/APS/B034/C404/D408/18	පිටකන්ද මාර්ගයේ තෙවන පටුම	158527.876/146838.288	158530.889/146838.527	158516.682/146572.202	158517.281/146575.142	301.63	3.0	2.5
248	SG/APS/B034/C404/D408/19	පිටකන්ද මාර්ගයේ සිව්වන පටුම	158391.624/146794.043	158394.664/146793.94	158383.118/146734.843	158383.936/146731.956	68.16	3.0	2.6
249	SG/APS/B034/C404/D408/20	පිටකන්ද මාර්ගයේ පස්වන පටුම	158371.028/146839.404	158370.205/146841.229	158389.514/146863.734	158387.878/146864.886	33.99	2.0	1.6
250	SG/APS/B034/C404/D408/21	පිටකන්ද මාර්ගයේ සයවන පටුම	158320.446/146865.636	158314.122/146867.684	157949.878/146559.532	157951.843/146556.634	1178.49	3.5	3.0
251	SG/APS/B034/C404/D408/21/01	පිටකන්ද මාර්ගයේ සයවන පටුමෙහි පළමු අතුවර මාර්ගය- අඩිපාර	157801.663/147049.828	157798.386/147047.874	157712.91/147152.417	157710.026/147153.239	165.53	3.0	2.5
252	SG/APS/B034/C404/D408/22	පිටකන්ද මාර්ගයේ ගම්පහ අඩිපාර	158185.44/146770.019	158188.761/146770.059	157934.147/146347.428	157935.373/146343.932	545.86	3.0	1.6
253	SG/APS/B034/C404/D408/23	පිටකන්ද මාර්ගයේ සයවන පටුම	158184.025/146774.431	158185.44/146770.019	157856.121/146923.467	157860.114/146923.231	434.81	4.0	1.0
254	SG/APS/B034/C404/D406/01	අඹගහ හංඳිය කළුමැදිය මාර්ගය	161131.443/145171.071	161134.896/145173.252	162750.019/144418.317	162752.289/144421.611	2582.81	4.0	3.0
255	SG/APS/B034/C404/D406/01/01	කළුමැදිය මාර්ගයේ පළමු පටුම	162224.666/144453.272	162227.802/144450.355	162240.579/144363.174	162241.403/144366.058	103.38	3.0	2.5
256	SG/APS/B034/C404/D406/01/02	කළුමැදිය මාර්ගයේ කන්ද කුට්ටිකන්ද මාර්ගය	162264.039/144484.394	162260.383/144487.966	164605.873/142928.664	164610.047/142928.024	3867.5	4.0	3.0
257	SG/APS/B034/C404/D406/01/02	කළුමැදිය මාර්ගයේ කන්ද කුට්ටිකන්ද මාර්ගයේ පළමු පටුම	164581.481/143010.128	164579.459/143013.662	164648.764/143122.174	164646.671/143125.582	137.74	4.0	3.0
258	SG/APS/B034/C404/D406/01/03	කළුමැදිය මාර්ගයේ දෙවන පටුම	162112.541/144752.893	162110.722/144749.256	161559.35/145069.992	161557.014/145066.745	667.89	4.0	3.5
259	SG/APS/B034/C404/D406/01/04	කළුමැදිය මාර්ගයේ තෙවන පටුම	162123.865/144753.511	162126.766/144755.492	162212.608/144716.623	162213.008/144720.099	99.83	3.5	3.0
260	SG/APS/B034/C404/D406/01/05	කළුමැදිය මාර්ගයේ සිව්වන පටුම	162370.841/144695.009	162366.643/144697.738	162578.124/144642.282	162581.031/144644.23	244.7	3.5	3.0

අනු අංකය	පාලනික කේතය	පාලන නම	ආරම්භක බණ්ඩාරක (කෙටි ලංකා)		අවසාන බණ්ඩාරක (කෙටි ලංකා)		පාලන දින (මිටර)	පාලන සාමාන්‍ය පළල (මිටර)	සංවර්ධන පළල (මිටර)
			වම	දකුණ	වම	දකුණ			
261	SG/APS/B034/C404/D406/02	අම්මන හංදිය ගමිසන මාර්ගය	161135.019/145178.676	161132.62/145175.212	161022.205/145644.805	161019.354/145641.999	557.3	4.0	2.5
262	SG/APS/B034/C404/D406/03	හැරැස්ස ගමිකන්දෙවන් මාර්ගය	161605.18/145371.611	161608.64/145371.892	162768.247/144927.2	162765.285/144927.678	1417.51	3.0	2.5
263	SG/APS/B034/C404/D406/03/01	හැරැස්ස ගමිකන්දෙවන් මාර්ගයේ පළමු පටුම	161723.374/145276.48	161725.7/145273.754	161612.773/145238.659	161612.75/145235.159	125.73	3.5	3.0
264	SG/APS/B034/C404/D406/03/02	හැරැස්ස ගමිකන්දෙවන් කළුමැදිය මාර්ගය	162368.317/144896.297	162375.609/144893.679	162499.257/144666.71	162502.681/144664.757	298.32	3.5	2.0
265	SG/APS/B034/C404/D406/04	දිග්ගල හැරැස්ස පළමු පටුම	161757.972/145517.095	161753.657/145517.637	161631.558/145673.812	161634.352/145672.721	324.09	3.0	2.5
266	SG/APS/B034/C404/D406/05	දිග්ගල හැරැස්ස දෙවන පටුම	161830.27/145488.7	161827.098/145490.218	161859.82/145549.14	161857.127/145551.377	70.26	3.5	3.0
267	SG/APS/B034/C404/D406/06	දිග්ගල හැරැස්ස තෙවන පටුම	162188.258/145563.453	162185.755/145561.775	161942.929/145692.707	161939.989/145693.305	307	3.0	2.5
268	SG/APS/B034/C404/D406/07	ගමිකන්ද පල්ලෙකඩ මාර්ගය	162742.986/145275.341	162740.918/145278.928	162286.339/145870.993	162287.869/145867.297	976.53	4.0	3.0
269	SG/APS/B034/C404/D406/07/01	ගමිකන්ද පල්ලෙකඩ මාර්ගයේ පළමු පටුම	162807.26/145344.143	162810.308/145346.885	162934.139/145311.753	162930.158/145312.137	163.63	4.0	2.5
270	SG/APS/B034/C404/D406/08	හැරැස්ස අක්කර 20 මාර්ගය	162781.233/145178.911	162783.57/145175.794	163371.974/144353.077	163372.966/144350.245	1227.93	3.0	2.5
271	SG/APS/B034/C404/D406/08/01	හැරැස්ස අක්කර 20 ගල්පොත්ත මාර්ගය	163169.07/144636.912	163172.194/144635.587	163154.466/144365.837	163156.867/144367.636	449.28	3.0	2.5
272	SG/APS/B034/C404/D406/09	දිග්ගල හැරැස්ස මාර්ගය	162982.034/145043.287	162978.825/145045.674	163923.35/144979.121	163920.473/144982.068	1085.36	4.0	3.0
273	SG/APS/B034/C404/D406/09/01	දිග්ගල මුකලාන මාර්ගය	163169.314/145100.199	163169.314/145100.199	163056.984/145390.869	163054.742/145388.875	379.65	3.0	2.0
274	SG/APS/B034/C404/D406/10	දිග්ගල හැරැස්ස සිව්වන පටුම	163495.456/144665.743	163490.517/144667.758	163580.059/144758.336	163580.113/144761.836	232.18	3.5	2.5
275	SG/APS/B034/C404/D406/11	දිග්ගල හැරැස්ස අතුරු මාර්ගය -අඩිපාර	163662.368/144590.539	163660.819/144591.402	163837.071/144889.362	163836.118/144888.003	405.69	1.5	1.0
276	SG/APS/B034/C404/D406/12	කුට්ටිකන්ද මාර්ගය	163664.449/144585.944	163667.172/144584.426	164044.067/144246.188	164044.113/144249.187	806.19	3.0	3.0

අනු අංකය	පාලනික කේතය	පාරේ නම	ආරම්භක බණ්ඩාංක (කදවල ශ්‍රී ලංකා)		අවසාන බණ්ඩාංක (කදවල ශ්‍රී ලංකා)		පාරේ දිග (මීටර්)	පාරේ සාමාන්‍ය පළල (මීටර්)	සංවර්ධිත පළල (මීටර්)
			වම	දකුණ	වම	දකුණ			
277	SG/APS/B034/C404/D406/12/01	කුට්ටිකන්ද උමංදොළ මාර්ගය	163639.496/144482.403	163639.278/144479.904	163494.483/144343.5	163496.523/144344.945	256.78	2.5	2.0
278	SG/APS/B034/C404/D407/01	ගවරිගිරිය වෙල්මණ්ඩිය හරහා මුනින්නන්ද මාර්ගයේ පළමු පටුම	160699.858/143935.506	160703.361/143935.567	160661.878/143848.602	160664.132/143845.925	105.65	3.5	3.0
279	SG/APS/B034/C404/D407/02	ගවරිගිරිය කොළඹුව මාර්ගය	160327.199/143850.242	160329.754/143845.734	158174.679/143543.167	158176.11/143540.53	4713.83	3.0	2.8
280	SG/APS/B034/C404/D407/02/01	ගම්පහ පළමු පටුම	160148.25/143158.168	160149.739/143161.848	160251.028/143076.245	160254.979/143076.863	140.62	4.0	3.0
281	SG/APS/B034/C404/D407/02/02	තැබ්බකන්ද මාර්ගය	159992.397/143096.675	159988.046/143097.569	158432.198/143398.985	158433.316/143395.136	2083.16	4.0	3.0
282	SG/APS/B034/C404/D407/02/01	කොදුගල මාර්ගය	158669.768/143759.738	158673.128/143762.179	158169.001/143726.865	158173.893/143724.586	1119.83	4.0	3.0
283	SG/APS/B034/C404/D407/02/02	තැබ්බකන්ද මාර්ගයේ පළමු පටුම	158454.333/143404.292	158459.596/143408.227	158565.735/143409.54	158564.696/143413.403	113.2	4.0	3.0
284	SG/APS/B034/C404/D407/02/03	නිශ්ශත බුලත්සිංහල මාර්ගය	159860.232/142810.67	159869.03/142810.453	160719.397/142209.444	160720.446/142213.304	1113.02	4.0	3.0
285	SG/APS/B034/C404/D407/02/01	නිශ්ශත බුලත්සිංහල මාර්ගයේ පළමු පටුම	160588.267/142272.567	160586.011/142274.583	160721.102/142641.984	160721.439/142644.966	924.49	3.0	2.6
286	SG/APS/B034/C404/D407/02/04	ගම්පහ බෝධිය තැබ්බකන්ද මාර්ගය	159758.823/142781.741	159754.918/142780.886	159730.077/143276.113	159727.642/143278.002	1077.1	3.0	3.0
287	SG/APS/B034/C404/D407/02/05	ගවරිගිරිය කොළඹුව මාර්ගයේ පළමු පටුම	159720.815/142722.739	159720.174/142719.347	159357.438/142973.765	159359.763/142971.87	515.98	3.0	2.7
288	SG/APS/B034/C404/D407/02/06	ගවරිගිරිය කොළඹුව මාර්ගයේ දෙවන පටුම	158383.129/143228.229	158383.713/143232.571	158576.865/143284.811	158574.171/143288.034	237.37	4.2	2.8
289	SG/APS/B034/C404/D407/02/07	ගවරිගිරිය කොළඹුව මාර්ගයේ තෙවන පටුම	158282.665/143540.767	158278.032/143541.949	158197.617/144086.884	158196.338/144089.597	652.69	3.0	3.0
290	SG/APS/B034/C404/D407/03	ගවරිගිරිය මුනින්නන්ද මාර්ගයේ පළමු පටුම	160070.308/144121.318	160074.095/144115.104	159968.153/144113.02	159970.943/144111.919	150.67	3.0	2.5

අනු අංකය	පාලනික කේතය	පාලන නම	ආරම්භක බණ්ඩාරක (කදවල ශ්‍රී ලංකා)		අවසාන බණ්ඩාරක (කදවල ශ්‍රී ලංකා)		පාලන දින (මිටර)	පාලන සාමාන්‍ය පළල (මිටර)	සංවර්ධන පළල (මිටර)
			වම	දකුණ	වම	දකුණ			
291	SG/APS/B034/C404/D407/04	ගෙවරිය මුනිකන්ද මාර්ගයේ දෙවන පටුම	159794.826/144264.634	159797.389/144263.063	159768.364/144244.475	159770.02/144241.973	36.26	3.0	2.5
292	SG/APS/B034/C404/D407/05	ගෙවරිය මුනිකන්ද මාර්ගයේ තෙවන පටුම	159666.649/144453.8	159663.63/144455.816	159807.424/144467.393	159805.364/144469.573	164.01	3.0	2.5
293	SG/APS/B034/C404/D407/06	ගෙවරිය මුනිකන්ද මාර්ගයේ සිව්වන පටුම	159448.12/144509.898	159444.09/144510.486	159608.707/144592.149	159610.995/144595.43	316.5	4.0	3.0
294	SG/APS/B034/C404/D407/06/01	ගෙවරිය මුනිකන්ද මාර්ගයේ සිව්වන පටුමගෙහි පළමු අතුරු මාර්ගය	159546.329/144610.2	159541.403/144611.997	159544.549/144642.438	159540.597/144643.056	35.18	4.0	3.0
295	SG/APS/B034/C404/D407/07	කොළඹ 04 මුනිකන්ද ඉහළ කන්ද මාර්ගය	158971.526/144597.328	158969.03/144594.416	158120.112/145533.83	158116.754/145532.053	1357.05	3.8	3.0
296	SG/APS/B034/C404/D407/07/01	කොළඹ 04 මුනිකන්ද ඉහළ කන්ද මාර්ගයේ පළමු පටු මාර්ගය	158847.003/144733.997	158845.258/144738.239	159039.194/144981.19	159036.634/144983.272	428.42	3.3	3.0
297	SG/APS/B034/C404/D407/07/02	කොළඹ 04 මුනිකන්ද දෙවැනි මාර්ගය	158696.391/144884.86	158699.492/144883.193	158634.513/144675.817	158636.259/144678.85	242.44	3.5	2.8
298	SG/APS/B034/C404/D407/07/03	කොළඹ 04 මුනිකන්ද පස්වන පටුම	158542.604/145028.014	158538.637/145030.686	158714.365/145131.924	158714.169/145134.917	392.11	3.0	2.5
299	SG/APS/B034/C404/D407/03/01	කොළඹ 04 මුනිකන්ද පස්වන පටුමගෙහි පළමු අතුරු මාර්ගය	158590.991/145201.086	158587.689/145201.461	158695.52/145353.7	158696.379/145356.574	601.07	3.0	2.5
300	SG/APS/B034/C404/D407/08	කොළඹ 04 මුනිකන්ද සයවන පටුම	158866.522/144388.389	158865.883/144385.255	158610.211/144338.245	158608.168/144336.049	291.71	3.0	2.5
301	SG/APS/B034/C404/C401/01	ලන්දේසියේ මාර්ගය	163569.417/141308.403	163565.619/141309.094	163332.674/141668.101	163331.132/141664.958	469.6	3.5	2.5
302	SG/APS/B034/C404/C401/02	දුම්මර මාර්ගය	163944.518/141303.777	163948.493/141304.248	166245.219/139702.94	166244.348/139706.936	3549.34	4.0	3.5
303	SG/APS/B034/C404/C401/02/01	මහලොවේ පහළ පළමු මාර්ගය	166002.781/139632.525	166010.627/139627.027	164611.691/139486.328	164611.307/139482.347	1750.26	4.0	2.5
304	SG/APS/B034/C404/C401/02/01/01	මහලොවේ බටහිර පළමු මාර්ගය	165888.461/139579.195	165892.671/139580.48	165866.895/139267.512	165870.825/139266.768	458.09	4.0	3.0

අනු අංකය	පාලනික කේතය	පාරේ නම	ආරම්භක බේන්දරය (කදවල ශ්‍රී ලංකා)		අවසාන බේන්දරය (කදවල ශ්‍රී ලංකා)		පාරේ දිග (මීටර්)	පාරේ සාමාන්‍ය පළල (මීටර්)	සංවර්ධිත පළල (මීටර්)
			වම	දකුණ	වම	දකුණ			
305	SG/APS/ B034/C404/ C401/02/01/02	මහවැලවත්ත පහළ දෙවන මාර්ගය	165627.987/139570.743	165623.85/139571.777	165642.93/139611.545	165640.391/139614.636	48.85	4.0	3.0
306	SG/APS/ B034/C404/ C401/02/01/03	මහවැලවත්ත බටහිර දෙවන මාර්ගය	165489.395/139597.805	165494.258/139595.241	165390.308/139350.989	165393.146/139353.809	406.11	4.0	2.5
307	SG/APS/ B034/C404/ C401/02/01/04	මහවැලවත්ත පහළ තෙවන මාර්ගය	165321.014/139668.669	165316.721/139668.115	165302.971/139736.613	165299.871/139734.989	72.95	3.5	2.5
308	SG/APS/ B034/C404/ C401/02/01/05	සෝදුරැකන්ද මාර්ගය	164924.12/139470.482	164918.59/139471.973	164709.911/139695.183	164708.337/139691.506	434.5	4.0	2.5
309	SG/APS/B034/ C404/C401/02/02	දුම්බර නො.02 මාර්ගය	166065.85/139574.914	166069.315/139571.639	167182.273/138722.521	167178.712/138720.7	2153.66	4.0	2.5
310	SG/APS/ B034/C404/ C401/02/02/01	දුම්බර නො.02 මාර්ගයේ පළමු පටුමෙහි පළමු අකුරු මාර්ගය	166130.695/139486.064	166134.467/139484.669	166278.353/139166.614	166282.224/139165.607	384.13	4.0	2.5
311	SG/APS/ B034/C404/ C401/02/02/01/01	දුම්බර නො.02 මාර්ගයේ පළමු පටුමෙහි පළමු අකුරු මාර්ගය	166146.247/139397.065	166152.835/139391.805	166076.601/139392.33	166075.03/139389.773	127.38	3.0	2.5
312	SG/APS/B034/ C404/C401/03	දුම්බර මානාන කුට්ටිකන්ද මාර්ගය	164164.67/141345.967	164158.941/141346.65	165891.23/142114.353	165896.228/142114.522	5413.49	5.0	2.5
313	SG/APS/B034/ C404/C401/03/01	නො.01 දුම්බර මානාන මාර්ගය	164536.479/141436.909	164537.5/141440.87	167409.194/139926.99	167413.289/139928.864	3909.45	4.0	2.5
314	SG/APS/B034/ C404/C401/03/02	දුම්බර මානාන පතල්මේදිය මාර්ගය	164380.898/141542.213	164377.625/141544.513	164052.052/142374.41	164051.034/142370.542	1216.5	4.0	2.6
315	SG/APS/ B034/C404/ C401/03/02/01	දුම්බර මානාන පතල්මේදිය මාර්ගයේ පළමු පටු මාර්ගය	164459.644/141680.811	164456.362/141678.194	164138.131/141911.672	164137.558/141907.714	427.07	4.0	3.0
316	SG/APS/ B034/C404/ C401/03/02/02	දුම්බර මානාන පතල්මේදිය මාර්ගයේ දෙවන පටු මාර්ගය	164531.977/141828.718	164529.88/141831.622	164643.566/142030.531	164640.092/142030.108	257.64	3.5	2.5

අනු අංකය	පාලනික කේතය	පාලන නම	ආරම්භක බණ්ඩාරක (කදවල ශ්‍රී ලංකා)		අවසාන බණ්ඩාරක (කදවල ශ්‍රී ලංකා)		පාලන දින (මිටර්)	පාලන සාමාන්‍ය පළල (මිටර්)	සංවර්ධන පළල (මිටර්)
			වම	දකුණ	වම	දකුණ			
317	SG/APS/B034/C404/C401/03/02/01	දුම්රි මාර්ග මාර්ගය	164636.291/141954.722	164634.939/141959.151	165198.71/141807.634	165202.07/141804.641	631.81	4.5	2.5
318	SG/APS/B034/C404/C401/03/02/03	දුම්රි මාර්ග පහළමණ්ඩිය මාර්ගයේ කෙටි පටු මාර්ගය	164258.957/142003.341	164262.152/141997.765	164100.798/142116.06	164099.281/142112.905	209.33	3.5	2.5
319	SG/APS/B034/C404/C401/03/03	දුම්රි මාර්ග කුට්ටිකන්ද මාර්ගයේ පළමු පටු මාර්ගය	163635.671/142357.046	163633.06/142355.555	163354.38/142662.842	163352.065/142660.933	437.79	3.0	2.5
320	SG/APS/B034/C404/C401/03/04	දුම්රි මාර්ග කුට්ටිකන්ද මාර්ගයේ දෙවන පටු මාර්ගය	163841.381/142762.389	163843.517/142765.997	164050.29/142644.156	164052.236/142640.66	284.95	4.0	2.6
321	SG/APS/B034/C404/C401/03/05	දුම්රි මාර්ග කුට්ටිකන්ද මාර්ගයේ දෙවන පටු මාර්ගය	164428.871/142945.801	164432.902/142942.32	164393.2/142868.601	164393.885/142864.66	122.87	4.0	3.0
322	SG/APS/B034/C404/C401/04	නො.82 කොඩිල අසල මාර්ගය	166942.524/139483.98	166935.276/139486.901	167628.782/139477.376	167628.157/139480.819	733.48	3.5	2.5
323	SG/APS/B034/C404/C401/05	දුම්රි මාර්ග නො.82 අඩි පාර	167105.569/139423.374	167107.583/139422.322	167227.378/138954.551	167229.145/138955.489	777.67	2.0	1.5
324	SG/APS/B034/C404/C401/06	දුම්රි මාර්ග නො.01 මාර්ගය	168182.573/138870.069	168182.06/138874.932	167809.426/140441.934	167805.474/140442.553	2313.73	4.0	3.0
325	SG/APS/B034/C404/C401/07	දුම්රි මාර්ග මැදිකැල්ල ඉහළ මාර්ගය	168219.125/138592.16	168214.867/138602.546	168972.466/138633.193	168973.006/138637.156	1081.8	4.0	2.5
326	SG/APS/B034/C404/C401/08	මිණිපුර දුම්රි මාර්ගය	168635.217/138228.821	168631.853/138226.142	168544.386/138262.959	168540.747/138261.297	115.54	4.0	3.0
327	SG/APS/B034/C404/C401/09	මිණිපුර දුම්රි මාර්ගය	168751.409/138073.939	168755.543/138073.175	168033.794/138501.759	168029.868/138502.53	1095.3	4.0	2.6
328	SG/APS/B034/C404/C401/10	පැණිගලවත්ත කොටුපොළ මාර්ගය	168799.218/137902.52	168802.731/137898.96	170067.609/137559.462	170064.276/137563.216	4084.85	5.0	2.6
329	SG/APS/B034/C404/C401/10/01	දුම්රි මාර්ග කළුමන මාර්ගය	168157.401/137774.094	168157.087/137769.89	167997.597/138114.812	167995.529/138117.635	472.76	3.5	2.5
330	SG/APS/B034/C404/C401/10/02	පැණිගලවත්ත කොටුපොළ මාර්ගයේ පළමු පටු මාර්ගය	168309.105/137506.554	168316.913/137504.135	168229.945/137508.79	168226.846/137506.262	98.39	4.0	3.0
331	SG/APS/B034/C404/C401/10/03	පැණිගලවත්ත කළුමන මාර්ගය	168712.289/137288.585	168716.23/137284.514	168665.296/137188.45	168669.989/137186.726	115.29	5.0	2.6


අනු අංකය	පාලනික කේතය	පාරේ නම	ආරම්භක බේන්දරය (කදවල ශ්‍රී ලංකා)		අවසාන බේන්දරය (කදවල ශ්‍රී ලංකා)		පාරේ දිග (මීටර්)	පාරේ සාමාන්‍ය පළල (මීටර්)	සංවර්ධිත පළල (මීටර්)
			වම	දකුණ	වම	දකුණ			
332	SG/APS/B034/C404/C401/10/04	පැණිගලවත්ත තොටුපොළ මාර්ගයේ දෙවන පටුම	168947.665/137212.914	168953.147/137210.257	168966.707/137126.2	168969.474/137128.342	101.26	3.5	2.0
333	SG/APS/B034/C404/C401/10/05	පැණිගලවත්ත තොටුපොළ මාර්ගයේ තෙවන පටුම	169420.173/137141.16	169423.788/137141.825	169384.294/136898.167	169387.592/136899.342	257.57	3.5	2.5
334	SG/APS/B034/C404/C401/10/06	පැණිගලවත්ත තොටුපොළ මාර්ගයේ සිව්වන පටුම	169946.902/137056.331	169951.315/137055.014	169858.152/136653.153	169858.993/136649.243	651.13	4.0	2.1
335	SG/APS/B034/C404/C401/10/07	පැණිගලවත්ත තොටුපොළ මාර්ගයේ පස්වන පටුම	169954.559/137054.354	169959.449/137054.23	170064.331/136947.26	170068.922/136946.957	176.83	4.6	4.0
336	SG/APS/B034/C404/C401/11	දොම්සියාවත්ත තොටුපොළ මාර්ගය	169590.917/138087.129	169585.055/138097.712	170081.326/137540.973	170084.233/137543.72	988.19	4.0	2.5
337	SG/APS/B034/C404/C401/12	මැදපොළ තො.01 මාර්ගය	169568.796/138653.691	169568.472/138644.097	167450.006/139959.141	167446.501/139953.649	2699.67	3.5	2.5
338	SG/APS/B034/C404/C401/13	පහළපොළ පළමු මාර්ගය	169603.301/138783.925	169616.912/138787.77	169853.565/138550.38	169855.909/138554.916	366.21	5.0	2.5
339	SG/APS/B034/C404/C401/14	පහළපොළ දෙවන මාර්ගය	169959.605/138553.252	169964.691/138549.087	170148.286/138438.809	170149.175/138442.708	455.02	4.0	3.0
340	SG/APS/B034/C404/C401/14/01	පහළපොළ දෙවන මාර්ගයේ පළමු පටුම	169880.599/138506.303	169884.09/138506.695	170065.251/138101.546	170068.631/138102.455	515.72	3.5	2.5
341	SG/APS/B034/C404/C401/14/02	පහළපොළ දෙවන මාර්ගයේ දෙවන පටුම	170042.718/138459.316	170045.674/138458.35	170006.107/138388.362	170008.808/138386.793	87.99	3.0	2.0
342	SG/APS/B034/C404/C401/14/03	පහළපොළ දෙවන මාර්ගයේ තෙවන පටුම	170120.979/138439.662	170123.481/138439.708	170025.403/138374.488	170027.377/138372.639	135.11	2.5	2.5
343	SG/APS/B034/C404/C401/15	පහළපොළ තෙවන මාර්ගය	170094.887/138614.153	170098.645/138615.552	170189.197/138604.204	170185.914/138606.488	120.09	4.0	2.5
344	SG/APS/B034/C404/C401/15/01	පහළපොළ තෙවන මාර්ගයේ පළමු පටුම	170108.994/138589.081	170111.809/138586.657	170121.508/138443.672	170124.792/138443.741	163.95	3.0	2.5
345	SG/APS/B034/C402/01	අයගම ඇලපාන මාර්ගයේ පළමු මාර්ගය	159461.777/149379.181	159458.973/149381.326	159387.298/149574.851	159385.347/149571.943	256.14	3.5	3.0
346	SG/APS/B034/C402/01/01	අයගම ඇලපාන මාර්ගයේ පළමු මාර්ගයේ පළමු අතුරු මාර්ගය	159423.585/149522.478	159424.399/149525.883	159502.077/149478.071	159503.732/149481.156	93.1	3.5	3.0


අනු අංකය	පාලනික කේතය	පාලන නම	ආරම්භක බණ්ඩාරක (කදවල ශ්‍රී ලංකා)		අවසාන බණ්ඩාරක (කදවල ශ්‍රී ලංකා)		පාලන දින (මිටර)	පාලන සාමාන්‍ය පළල (මිටර)	සංවර්ධන පළල (මිටර)
			වම	දකුණ	වම	දකුණ			
347	SG/APS/B034/C402/02	සරත්පුරය මැද මාර්ගය	159447.649/149388.194	159450.001/149384.943	159232.965/149320.121	159236.74/149318.507	300.32	4.0	3.0
348	SG/APS/B034/C402/02/01	සරත්පුරය මැද මාර්ගයේ පළමු පටුම	159382.923/149306.953	159382.727/149304.453	159306.148/149352.255	159304.278/149350.595	93.78	2.5	1.0
349	SG/APS/B034/C402/02/02	සරත්පුරය මැද මාර්ගයේ දෙවන පටුම	159255.574/149335.976	159252.454/149334.811	159277.353/149390.737	159276.866/149393.697	66.48	3.0	3.0
350	SG/APS/B034/C402/03	සරත්පුරය පළමු පටුම	159381.676/149465.264	159383.42/149462.67	159240.917/149429.631	159241.003/149426.547	155.78	3.0	3.0
351	SG/APS/B034/C402/04	අයගම ඇලපාන මාර්ගයේ දෙවන මාර්ගය	159389.948/149582.055	159387.143/149580.654	159326.662/149723.997	159323.688/149723.605	197.56	3.0	3.0
352	SG/APS/B034/C402/05	අයගම ඇලපාන මාර්ගයේ තෙවන මාර්ගය	159537.463/149681.071	159537.114/149684.57	159592.073/149643.185	159591.783/149646.672	75.32	3.5	3.5
353	SG/APS/B034/C402/06	අයගම ඇලපාන මාර්ගයේ සිව්වන මාර්ගය	159510.747/149768.346	159511.485/149764.748	159257.203/149882.453	159256.039/149879.153	316.02	3.5	3.5
354	SG/APS/B034/C402/07	සමරුගම මැද මාර්ගය	159379.418/149957.766	159379.92/149954.302	159165.735/149699.736	159169.01/149701.016	493.07	3.5	3.0
355	SG/APS/B034/C402/08	අයගම ඇලපාන මාර්ගයේ පස්වන මාර්ගය	159279.654/150104.126	159277.422/150106.134	159689.449/149943.843	159686.7/149945.045	505.46	3.0	3.0
356	SG/APS/B034/C402/09	අයගම ඇලපාන මාර්ගයේ සයවන මාර්ගය	159128.731/150373.43	159126.751/150370.511	158792.732/150542.001	158795.844/150540.399	578.75	3.5	3.0
357	SG/APS/B034/C402/10	අයගම ඇලපාන මාර්ගයේ සත්වන මාර්ගය	159741.171/150667.187	159740.058/150670.378	160130.92/150920.892	160129.531/150923.551	613.49	3.0	3.0
358	SG/APS/B034/D401/01	උඩුගල ගොදුර මාර්ගය	157287.745/150320.142	157291.64/150321.053	156313.654/146716.075	156316.312/146713.085	5197.59	4.0	3.5
359	SG/APS/B034/D401/01/01	උඩුගල මාර්ගය	157208.055/150206.886	157209.151/150203.024	156709.13/150088.967	156713.044/150089.79	1057.62	4.0	4.0
360	SG/APS/B034/D401/01/02	උඩුගල මාර්ගයේ ජනපදය මාර්ගය	157320.013/149886.172	157317.269/149883.871	156982.264/149661.686	156985.239/149659.842	566.71	3.5	3.0
361	SG/APS/B034/D401/01/02/01	උඩුගල මාර්ගයේ ඉහළ මාර්ගය	157227.648/149894.143	157225.013/149892.709	157160.356/149888.568	157163.081/149887.312	95.31	3.0	3.0


අනු අංකය	පාලනික කේතය	පාරේ නම	ආරම්භක බණ්ඩාංක (කාදවල ශ්‍රී ලංකා)		අවසාන බණ්ඩාංක (කාදවල ශ්‍රී ලංකා)		පාරේ දිග (මීටර්)	පාරේ සාමාන්‍ය පළල (මීටර්)	සංවර්ධිත පළල (මීටර්)
			වම	දකුණ	වම	දකුණ			
362	SG/APS/B034/ D401/01/02/02	තයිනිල් ජනපදය ගෙදර මාර්ගය	157133.609/149725.826	157137.132/149726.868	157065.731/149589.514	157069.925/149590.522	159.34	3.0	2.0
363	SG/APS/B034/ D401/01/02/03	තයිනිල් ජනපදය ගෙදර මාර්ගයේ පළමු පටුම	157030.221/149714.53	157027.327/149713.727	156910.603/149791.995	156908.828/149789.577	189.46	3.0	3.0
364	SG/APS/B034/ D401/01/03	උඩුගල පිටකන්ද ගම්පහා පළමු මාර්ගය	157326.54/149849.629	157323.621/149852.496	157404.109/149821.606	157407.586/149823.594	114.46	4.0	3.0
365	SG/APS/B034/ D401/01/04	උඩුගල පිටකන්ද ගම්පහා දෙවන මාර්ගය	157324.255/149782.296	157324.224/149785.299	157456.781/149792.983	157456.728/149795.982	155.48	3.0	3.0
366	SG/APS/B034/ D401/01/05	බුබුලෙන්ක මාර්ගය	157310.794/149645.707	157312.533/149648.173	157543.494/149446.695	157542.715/149449.591	352.37	3.0	2.0
367	SG/APS/B034/ D401/01/06	උඩුගල ගෙදර ගම්පහා මාර්ගය	157154.466/149534.557	157151.607/149533.449	156816.662/149478.874	156818.62/149481.149	472.18	3.0	2.0
368	SG/APS/B034/ D401/01/07	කළුතර එළවැල්ලෙන් මාර්ගය	156822.356/149378.184	156821.703/149375.114	156698.037/149406.824	156696.315/149404.368	132.69	3.0	3.0
369	SG/APS/B034/ D401/01/08	උඩුගල ගෙදර මාර්ගයේ පළමු පටුම	156811.451/149337.844	156811.69/149334.842	156763.994/149303.041	156765.413/149300.397	63.81	3.0	3.0
370	SG/APS/B034/ D401/01/09	ගෙදර පරණ ගම්පහා මාර්ගය	156684.691/148304.064	156681.118/148302.226	156549.574/148301.897	156552.931/148304.161	182.36	4.0	4.0
371	SG/APS/B034/ D401/01/10	ගෙදර ආරණ්‍ය මාර්ගය	156663.245/147217.589	156663.011/147221.128	156856.926/147066.015	156858.919/147068.892	256.08	3.5	3.0
372	SG/APS/B034/ D401/01/11	ගෙදර තනිවැස්ක මාර්ගය	156531.734/147168.814	156534.705/147170.276	156588.076/146855.55	156590.973/146856.33	350.74	3.0	2.5
373	SG/APS/B034/ D401/01/12	ගෙදර මිල්ලෙන්ක අඩිපාර	156514.649/147164.072	156512.859/147162.653	156399.529/147315.415	156397.529/147315.453	267.89	2.0	1.0
374	SG/APS/B034/ D401/01/13	ගෙදර මිල්ලෙන්ක මාර්ගය	156465.693/147104.555	156464.318/147100.354	155868.854/147300.375	155871.845/147303.031	1164.3	4.0	3.0
375	SG/APS/B034/ D401/01/13/01	ගෙදර මිල්ලෙන්ක මාර්ගයේ පළමු පටුම	155798.488/147446.75	155800.358/147442.241	155757.427/147412.9	155760.911/147413.242	106.04	3.5	2.5
376	SG/APS/B034/ D401/01/14	පුල්කිරිදොළ බලාගාරය මාර්ගය	156317.778/146714.349	156320.348/146716.86	157384.536/146089.61	157388.032/146089.765	1505.66	3.5	2.5


අනු අංකය	පාලනික කේතය	පාලන නම	ආරම්භක බණ්ඩාරක (කෙටි ලංකා)		අවසාන බණ්ඩාරක (කෙටි ලංකා)		පාලන දින (මිටර)	පාලන සාමාන්‍ය පළල (මිටර)	සංවර්ධන පළල (මිටර)
			වම	දකුණ	වම	දකුණ			
377	SG/APS/B034/ D401/02	උඩුගල අඟුරුවෙල මාර්ගයේ පළමු පටුම	157148.367/150420.874	157150.959/150419.323	156956.706/150276.248	156955.504/150273.499	276.08	3.0	3.0
378	SG/APS/B034/ D401/02/01	ශ්‍රී ධර්මපරික්ෂිතමය මාර්ගය	157080.52/150372.702	157078.667/150369.666	157022.099/150382.247	157020.6/150379.648	61.74	3.0	3.0
379	SG/APS/B034/ D401/03	උඩුගල අඟුරුවෙල මාර්ගයේ දෙවන පටුම	156827.768/150588.171	156824.818/150587.482	156791.117/150679.513	156788.524/150678.006	102.04	3.0	3.0
380	SG/APS/B034/ D401/04	අඟුරුවෙල ආරක්ෂිත පළමු මාර්ගය	156693.755/150550.761	156696.529/150551.993	156751.097/150216.214	156753.191/150218.367	546.79	3.0	2.5
381	SG/APS/B034/ D401/05	උඩුගල අඟුරුවෙල මාර්ගයේ තෙවන පටුම	156584.485/150624.643	156582.288/150627.259	156643.239/150734.101	156640.736/150732.446	153.86	3.0	2.5
382	SG/APS/B034/ D401/06	හඳුන්කන්ද බටහේන මාර්ගය	156040.438/150792.897	156036.998/150795.111	156122.938/150988.518	156122.743/150992.513	327.12	4.0	2.6
383	SG/APS/B034/ D401/06/01	හඳුන්කන්ද බටහේන මාර්ගයේ පළමු පටුම	156062.901/151020.222	156058.403/151020.36	156121.892/151137.242	156119.409/151140.995	157.53	4.5	2.0
384	SG/APS/B034/ D401/07	හඳුන්කන්ද පාසල් මාර්ගය	155993.968/150808.67	155990.983/150808.333	155932.163/150913.026	155929.876/150914.969	152.82	3.0	2.0
385	SG/APS/B034/ D401/08	හඳුන්කන්ද පළමු පටුම	155941.04/150567.698	155942.719/150571.068	156052.536/150397.226	156055.058/150399.652	219.62	3.5	2.5
386	SG/APS/B034/ D401/09	අඟුරුවෙල ආරක්ෂිත දෙවන මාර්ගය	155416.689/150299.172	155423.355/150297.887	156700.848/150198.96	156696.86/150194.851	2147.1	4.0	2.5
387	SG/APS/B034/ D401/10	උඩුගල අඟුරුවෙල මාර්ගයේ සිව්වන පටුම	155255.126/150278.066	155258.442/150279.193	155301.796/150099.024	155303.867/150101.844	238.52	3.5	3.0
388	SG/APS/B034/ D401/11	අඟුරුවෙල වැකිය අඩිපාර	154924.975/150380.579	154922.681/150383.016	154917.22/151066.195	154917.112/151069.193	975.28	3.0	2.0
389	SG/APS/B034/ D401/12	පන්විලහේන පළමු පටුම	154663.695/150905.562	154663.531/150901.319	154547.724/151089.588	154544.204/151091.487	247.05	4.0	3.0
390	SG/APS/B034/ D401/13	අඟුරුවෙල පන්විලහේන මාර්ගය	154671.092/150934.792	154668.105/150935.088	154379.255/151278.751	154379.522/151275.763	586.84	3.0	3.0
391	SG/APS/B034/ D401/13/01	පන්විලහේන දෙවන පටුම - අඩිපාර	154643.94/151182.473	154640.685/151184.567	154534.83/151309.855	154534.658/151306.859	211.24	3.0	1.0


අනු අංකය	පාලනික කේතය	පාලන නම	ආරම්භක බණ්ඩාංක (කාදවල ශ්‍රී ලංකා)		අවසාන බණ්ඩාංක (කාදවල ශ්‍රී ලංකා)		පාලන දින (මිටර්)	පාලන සාමාන්‍ය පළල (මිටර්)	සංවර්ධිත පළල (මිටර්)
			වම	දකුණ	වම	දකුණ			
392	SG/APS/B034/C403/01	වේරගමකන්ද මාර්ගය	153527.299/154057.44	153527.251/154061.441	154282.721/153664.727	154279.844/153667.505	989.79	4.0	4.0
393	SG/APS/B034/C403/02	කුකුළුවා රජමහා විහාර පළමු මාවත	153415.092/154520.334	153416.359/154526.083	154548.876/155593.224	154549.724/155596.62	2129.06	3.5	3.0
394	SG/APS/B034/C403/02/01	කරවිලගේන්ද්‍රය මාර්ගය	153688.552/154709.874	153688.286/154714.284	153796.476/154135.909	153799.374/154136.687	788.25	3.0	2.5
395	SG/APS/B034/C403/03	වැල්ලවත්ත නාවික මාර්ගය	153491.897/154877.567	153490.694/154874.125	153259.975/154932.132	153257.195/154930.006	306.89	3.5	3.0
396	SG/APS/B034/C403/04	කුකුළුවා රජමහා විහාර අඩිපාර	153515.858/154959.691	153515.612/154961.225	153738.21/155002.228	153738.768/155003.684	247.55	1.5	1.5
397	SG/APS/B034/C403/05	නාවිකවත්ත දේවාල මාර්ගය	153482.602/155076.016	153484.102/155072.29	153258.283/155086.651	153261.462/155085.185	312.38	3.5	3.5
398	SG/APS/B034/C403/06	නාවිකවත්ත කුරහන මාර්ගය	153329.396/155519.527	153332.445/155516.448	153150.443/155626.267	153150.56/155630.266	364.51	4.0	3.0
399	SG/APS/B034/C403/06/01	නාවිකවත්ත මඩිත්ත මාර්ගය	153156.402/155509.905	153159.597/155508.082	152728.705/155356.83	152726.554/155354.461	1343.14	3.2	3.0
400	SG/APS/B034/C403/07	පිඬුර කලවාන මාර්ගය	153417.591/155745.569	153416.569/155740.593	152709.9/156242.322	152708.631/156237.485	1060.64	5.0	4.0
401	SG/APS/B034/C403/07/01	තැන්නගේන මාර්ගය	152870.605/156202.46	152865.714/156201.659	153234.208/156678.36	153231.423/156675.489	1137.57	4.0	3.0
402	SG/APS/B034/C403/08	කුකුළුවා විහාර රජමහා විහාර දෙවන මාවත	153463.565/156000.401	153462.728/156003.372	154024.251/155442.209	154026.865/155440.112	864.91	3.0	3.0
403	SG/APS/B034/C403/09	පිඬුර කරවිට මාර්ගයේ පළමු දෙවන මාවත	153460.226/156158.501	153460.447/156165.711	153510.578/156229.595	153508.374/156232.314	90.02	3.5	3.0
404	SG/APS/B034/C403/10	පිඬුර කරවිට මාර්ගයේ දෙවන පළමු	153459.349/156263.282	153460.227/156267.562	153532.008/156308.444	153530.977/156311.79	89.52	3.5	3.0
405	SG/APS/B421/C428/01	කුකුළුවා රජමහා විහාර මාර්ගයේ පළමු මාර්ගය	153463.408/150016.386	153462.085/150021.274	154167.955/149520.647	154171.478/149517.099	979.21	5.0	3.0
406	SG/APS/B421/C428/02	නිදහස පන්සල මාර්ගය	153121.918/149082.771	153121.754/149078.768	152640.684/149889.154	152636.832/149890.232	1216.06	4.0	2.5

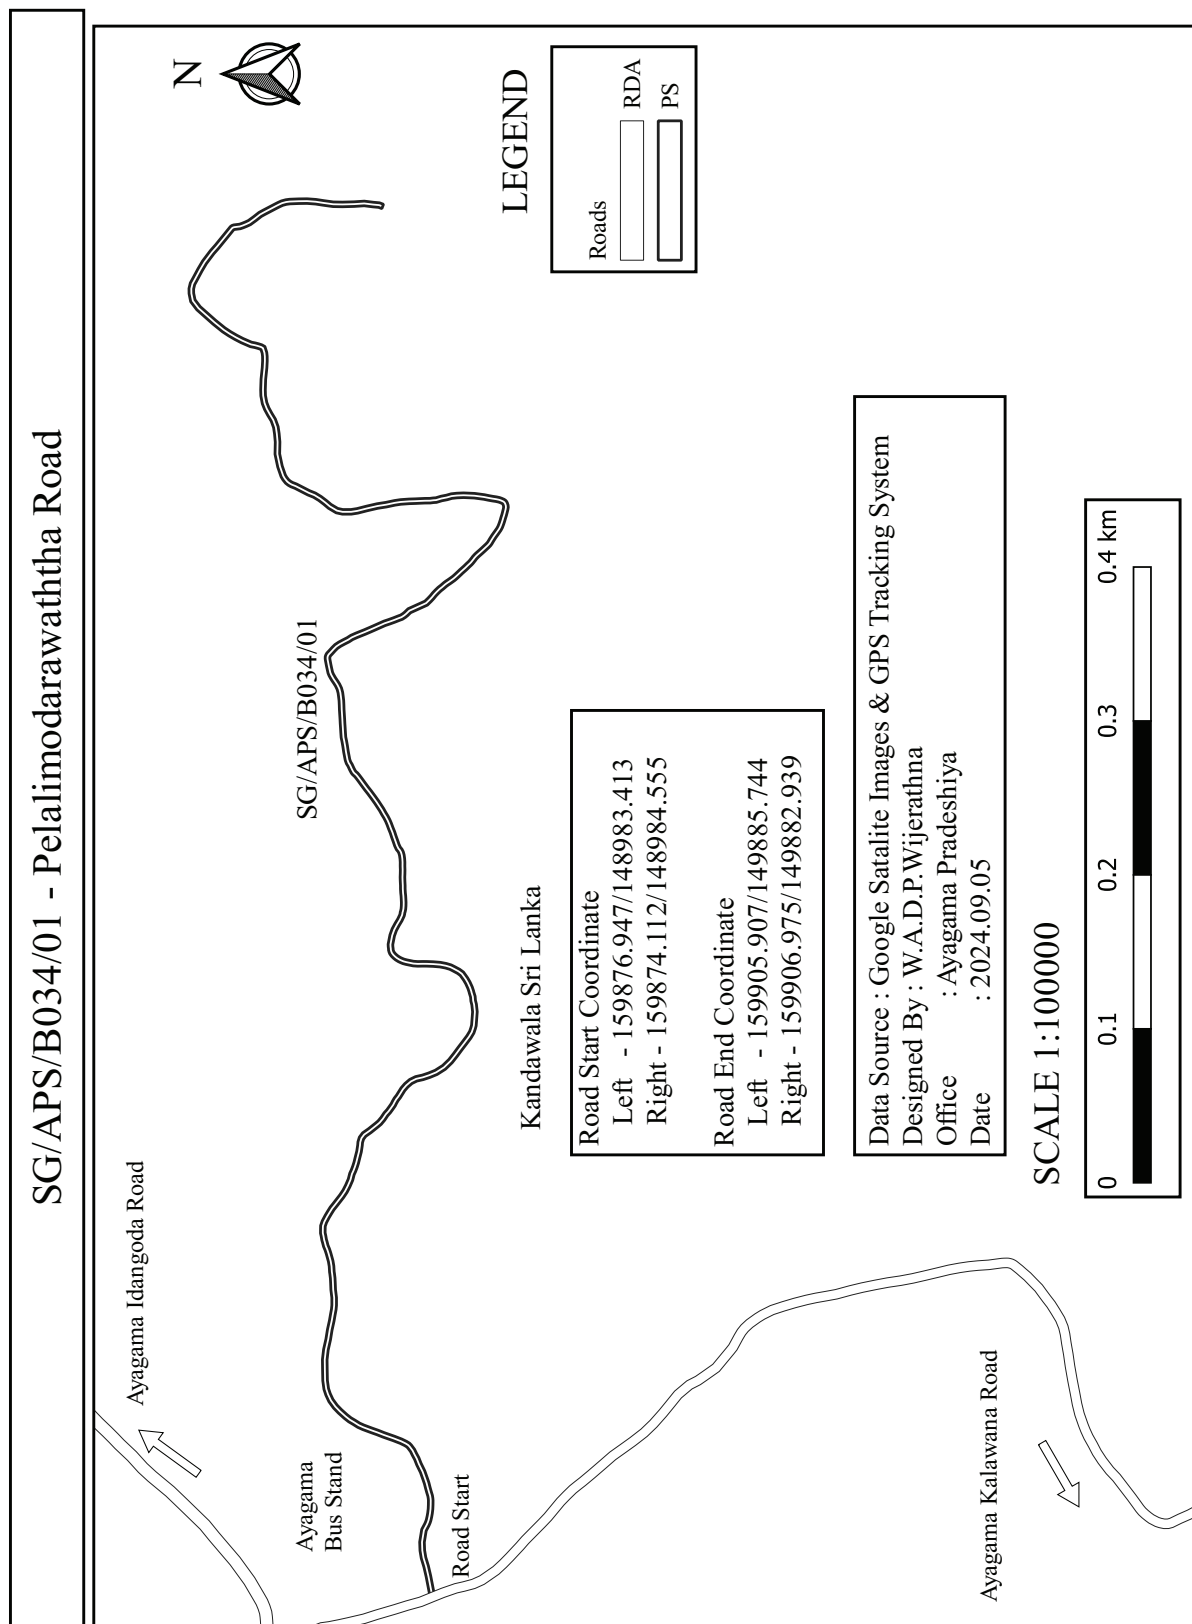


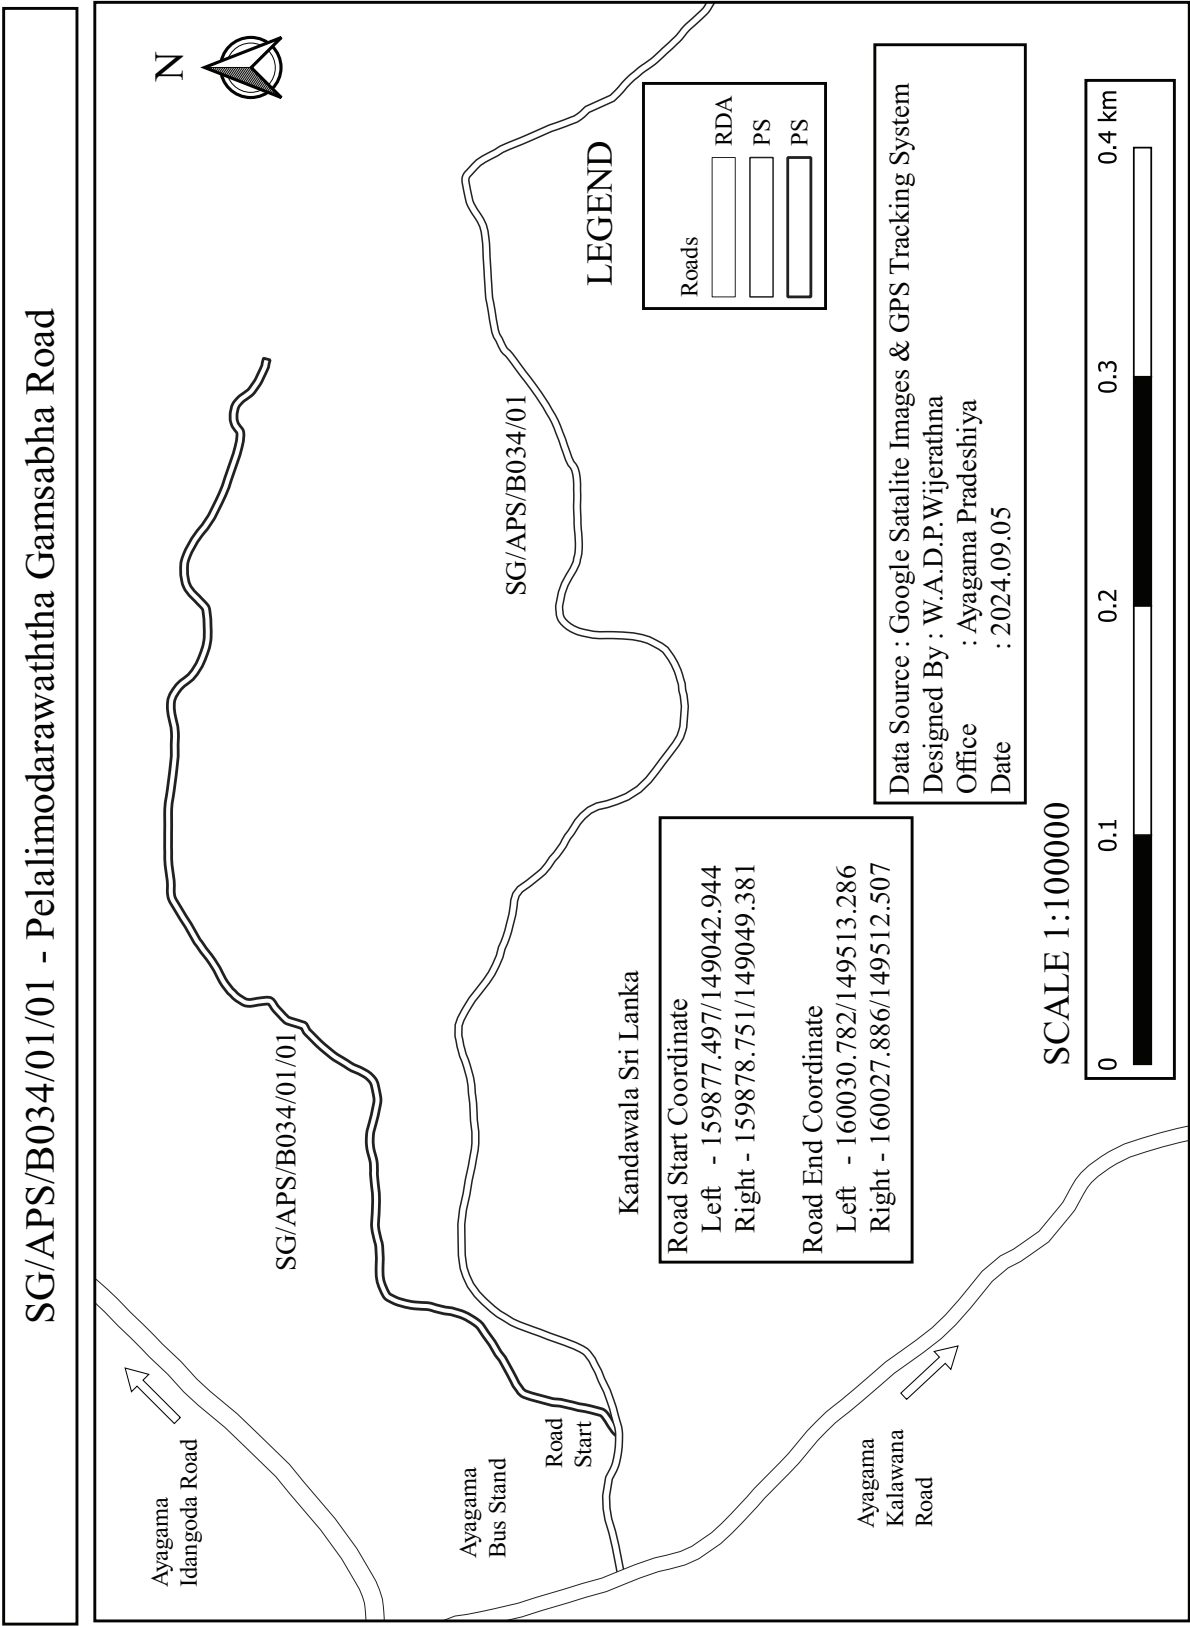


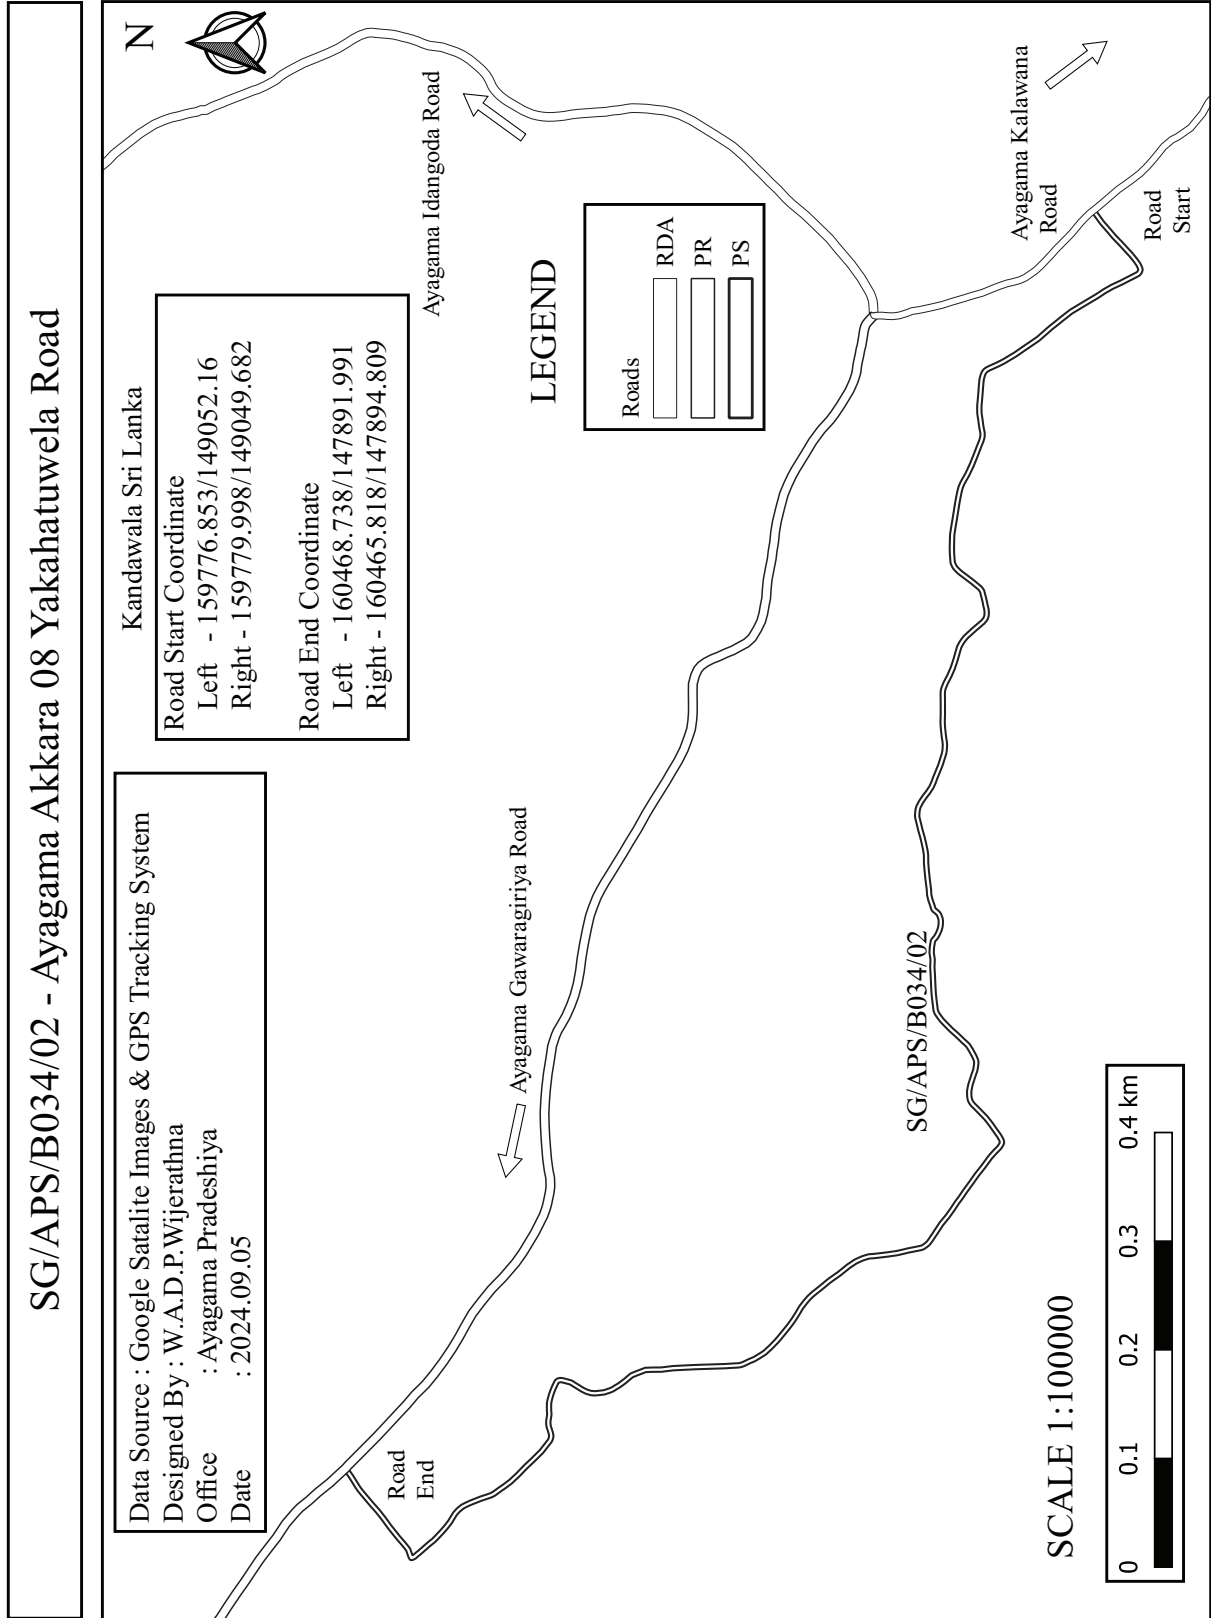


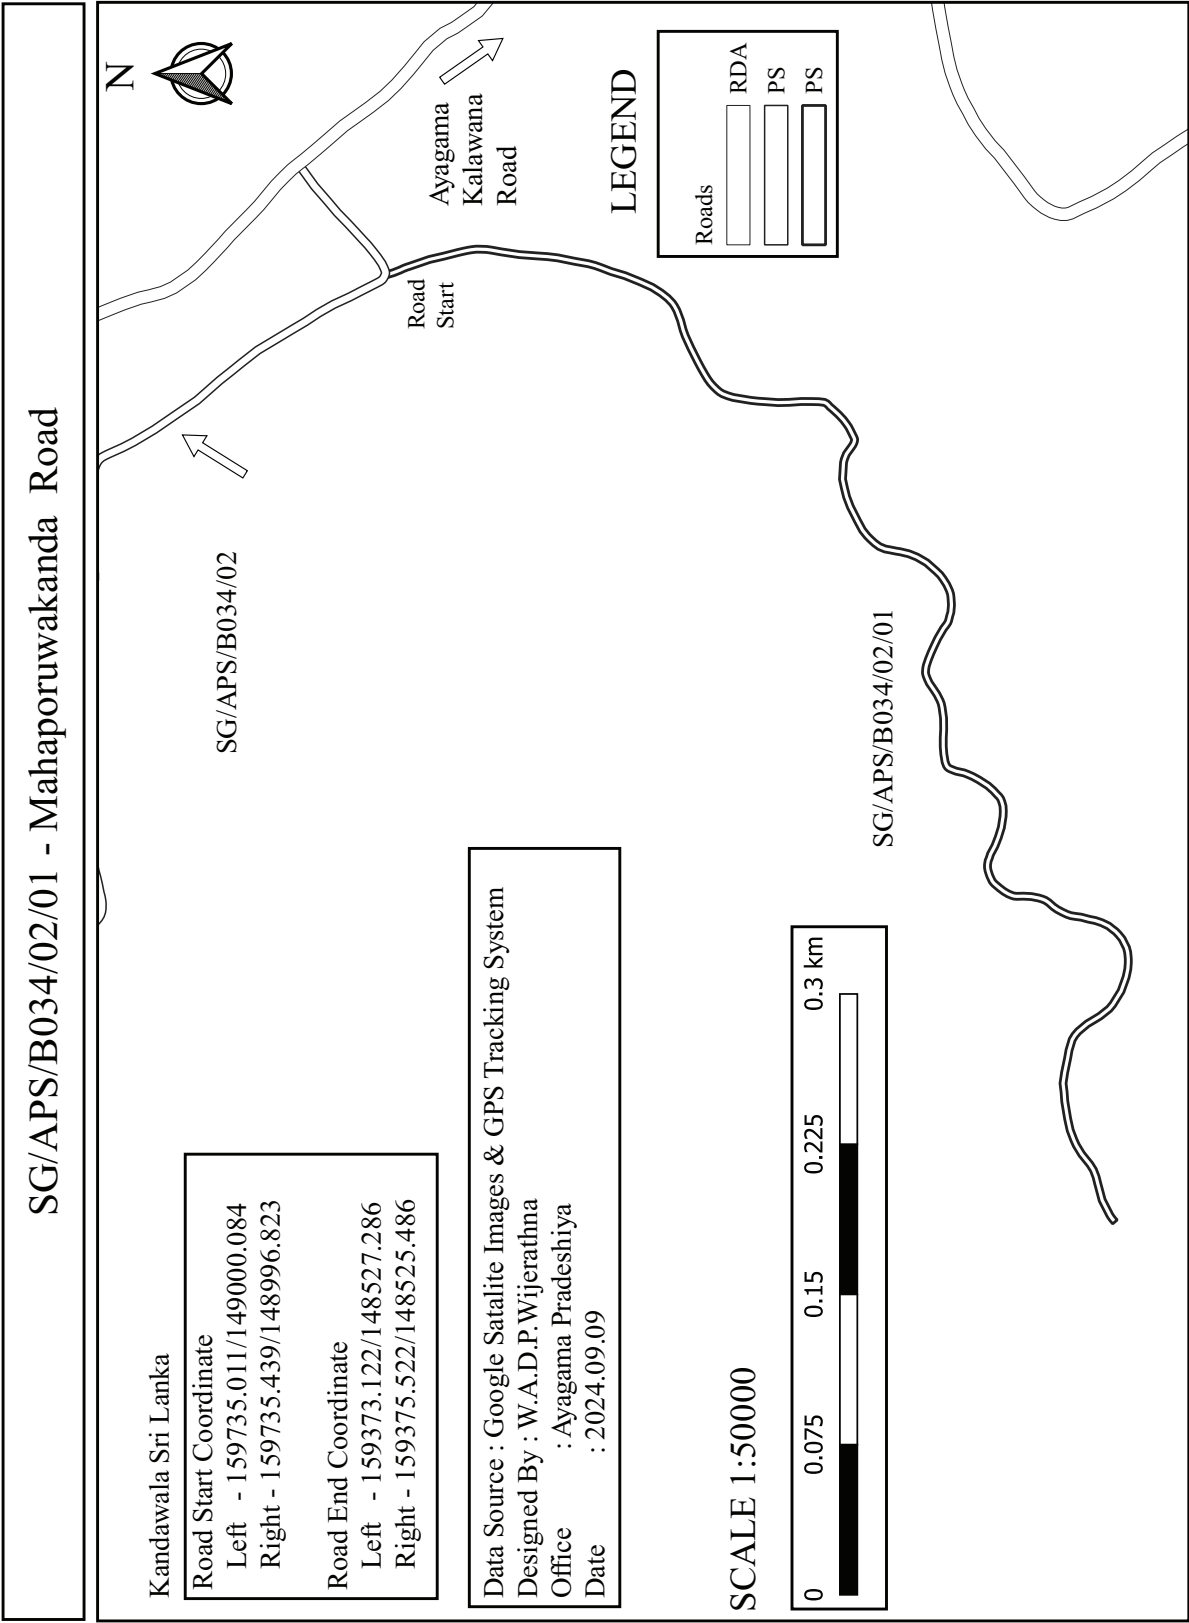


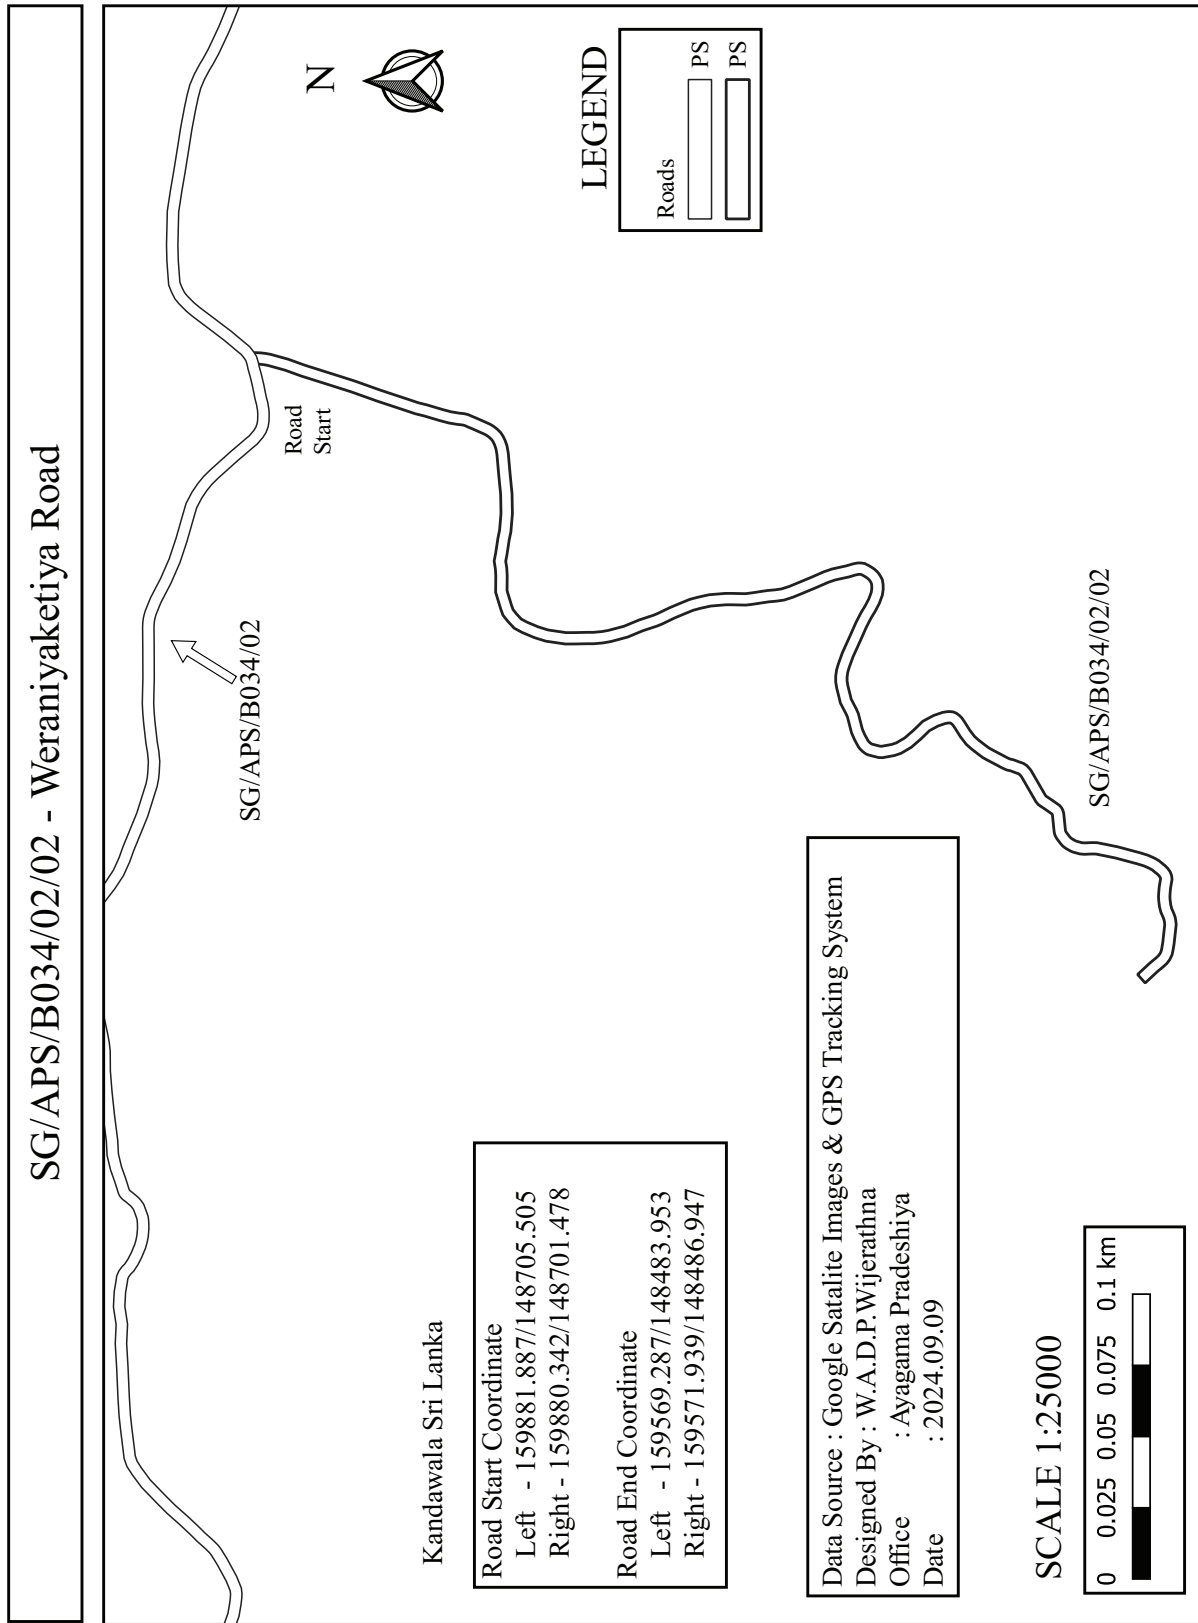


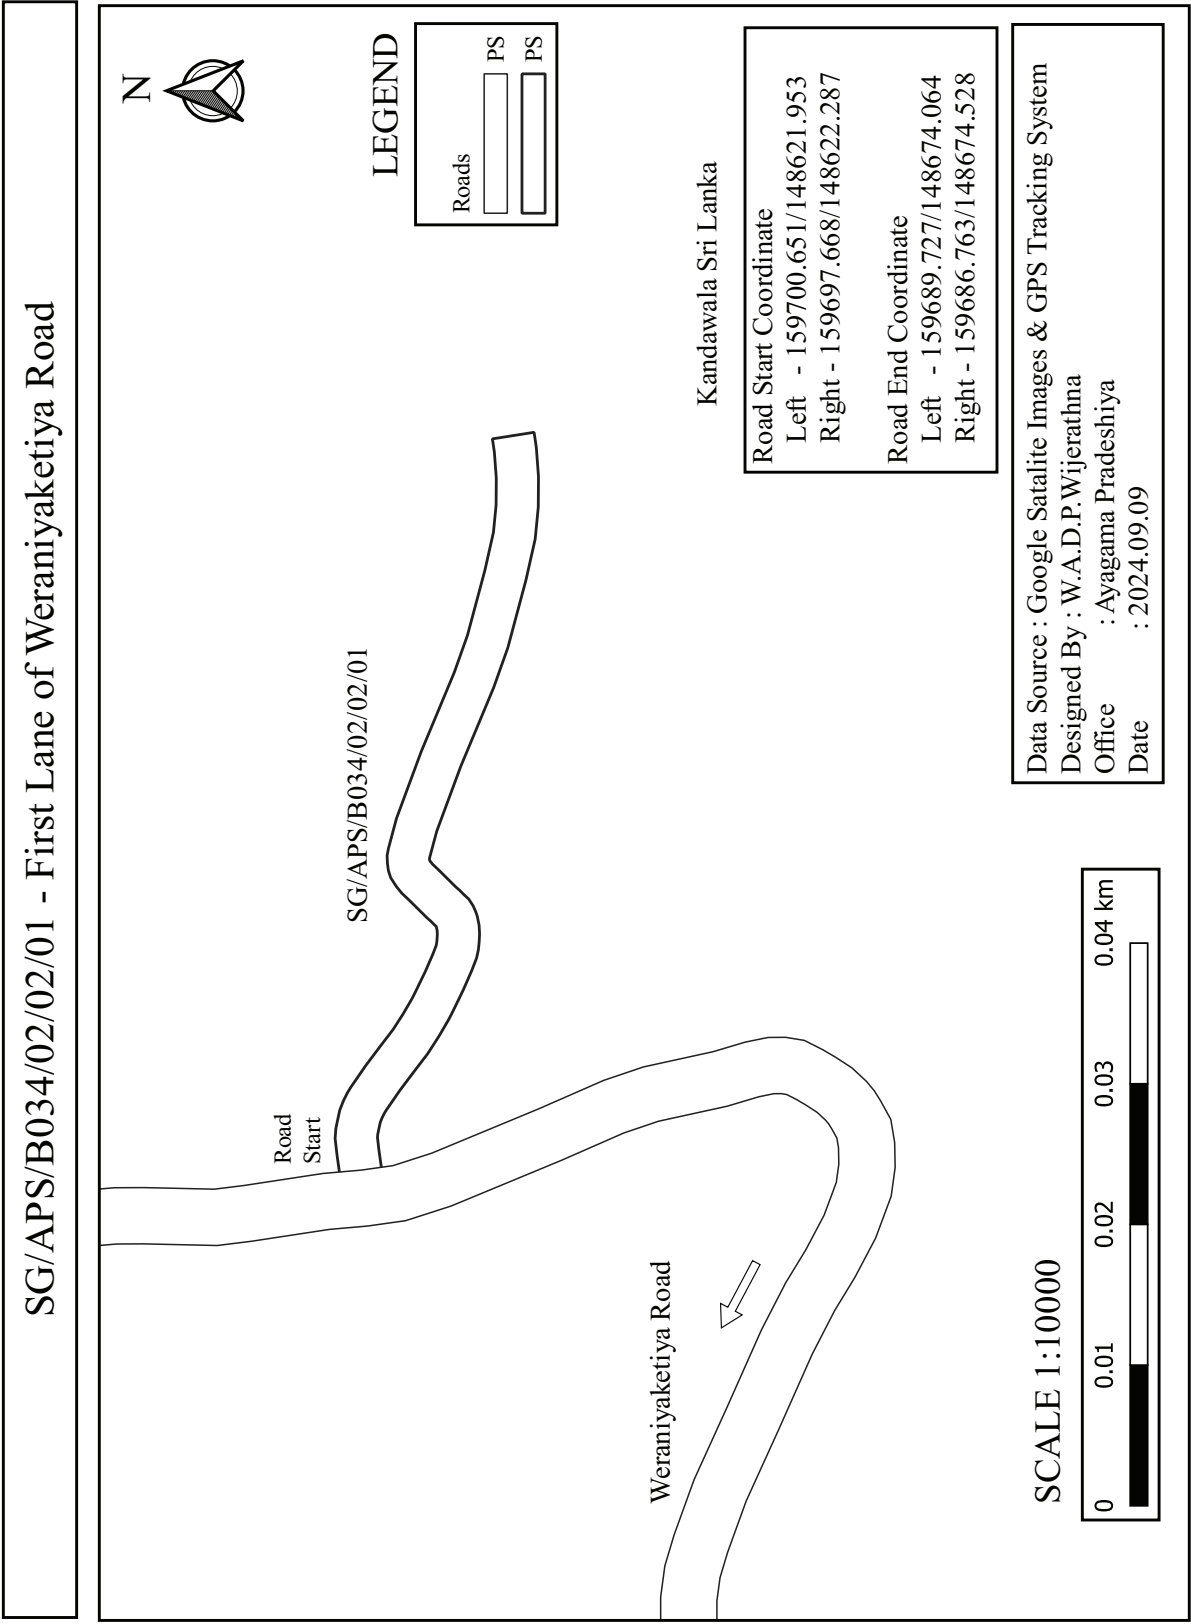


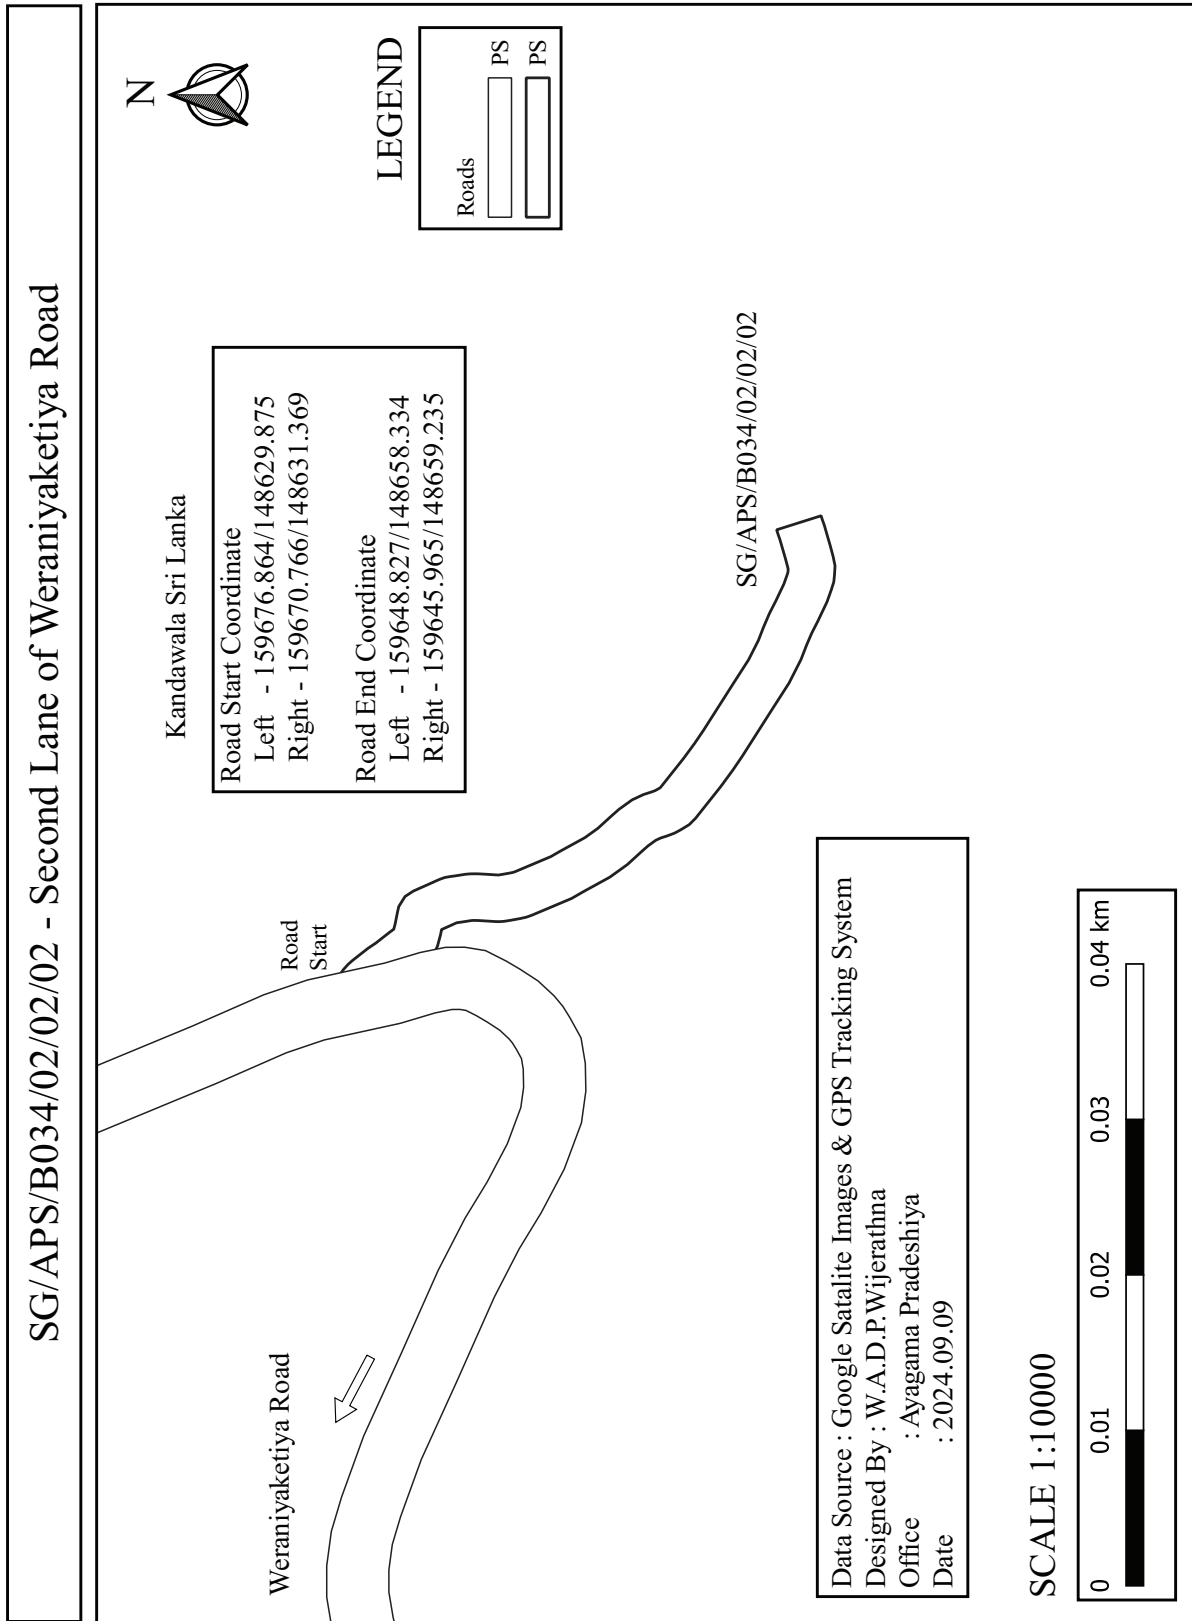


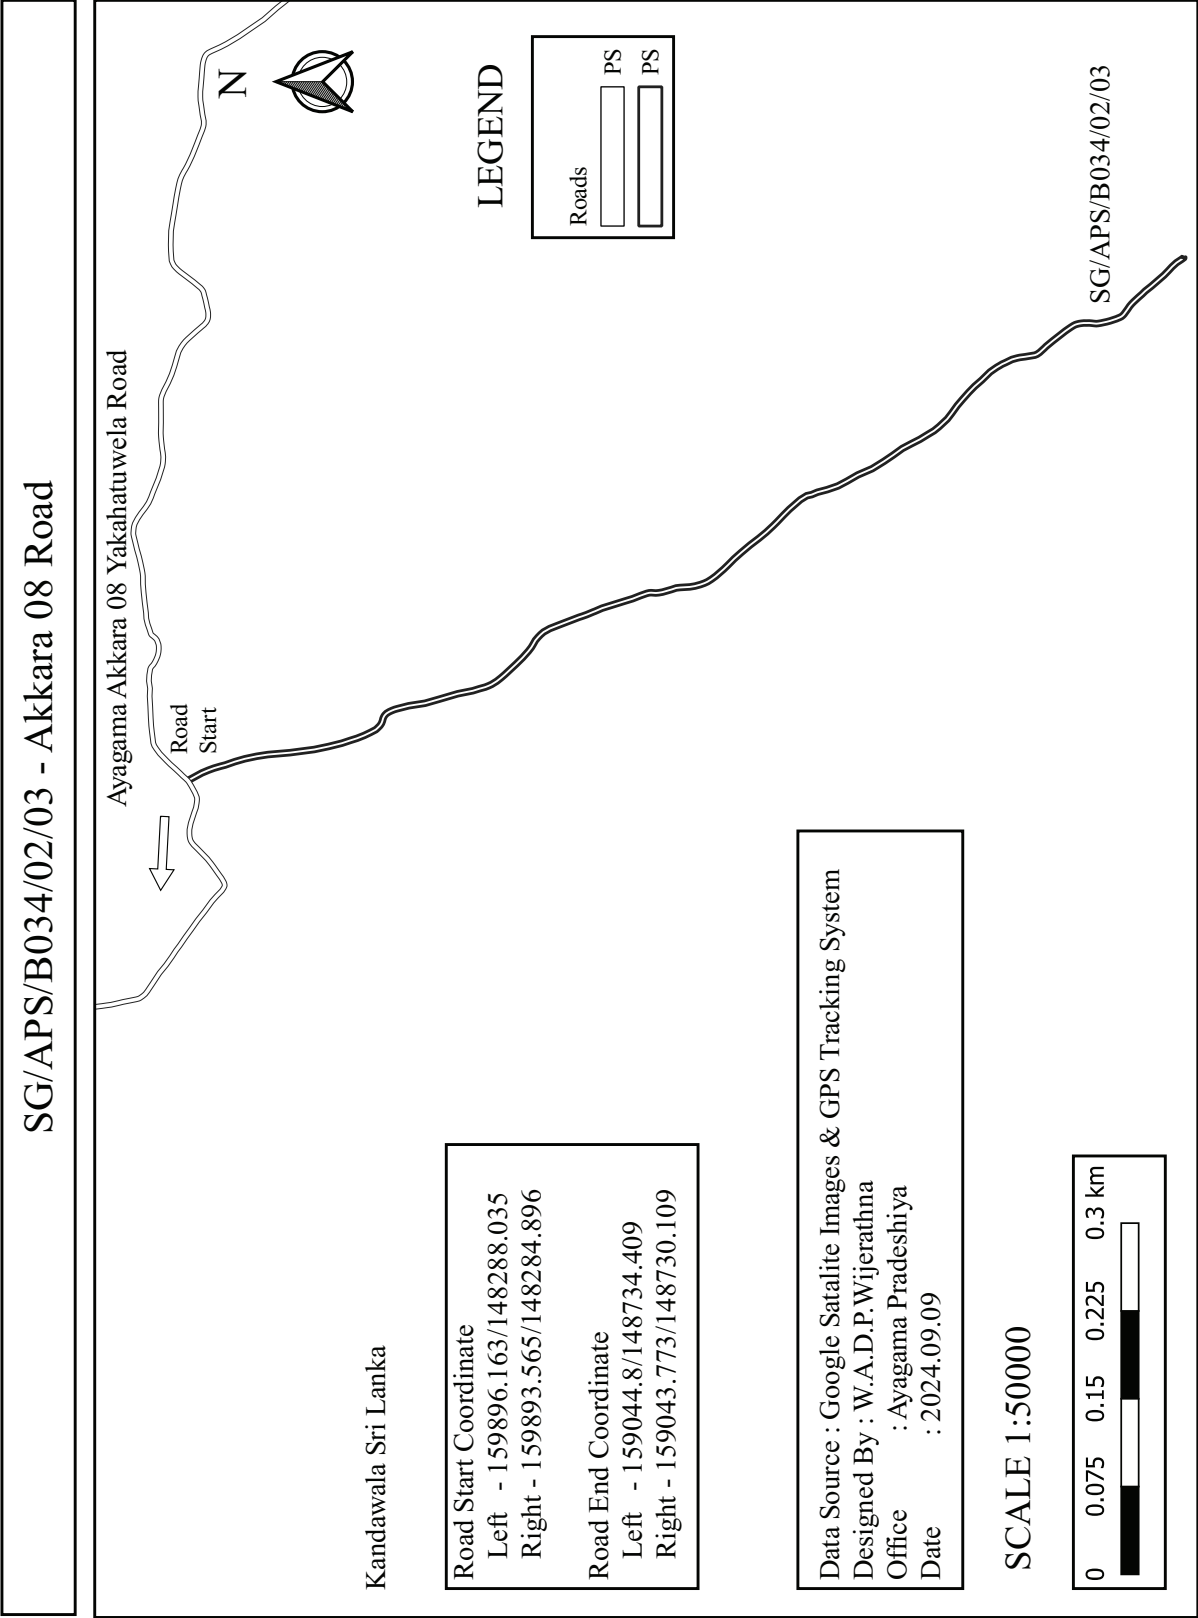


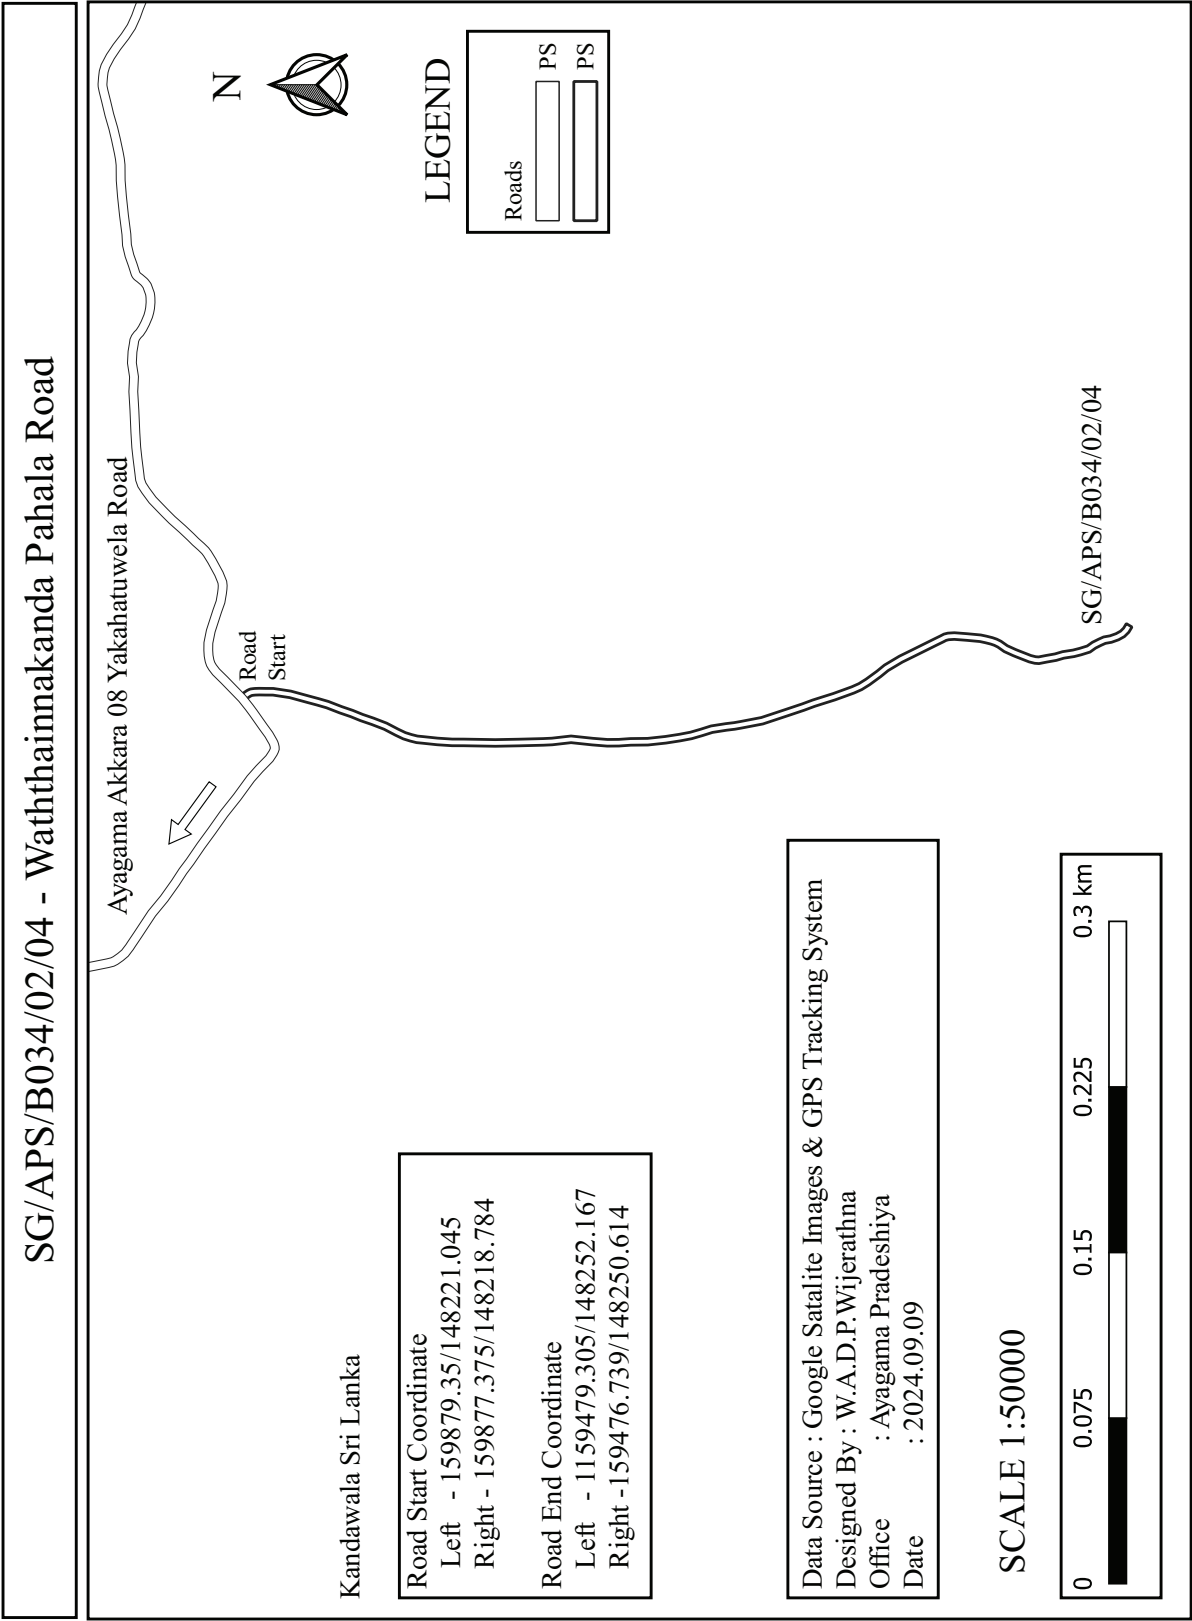


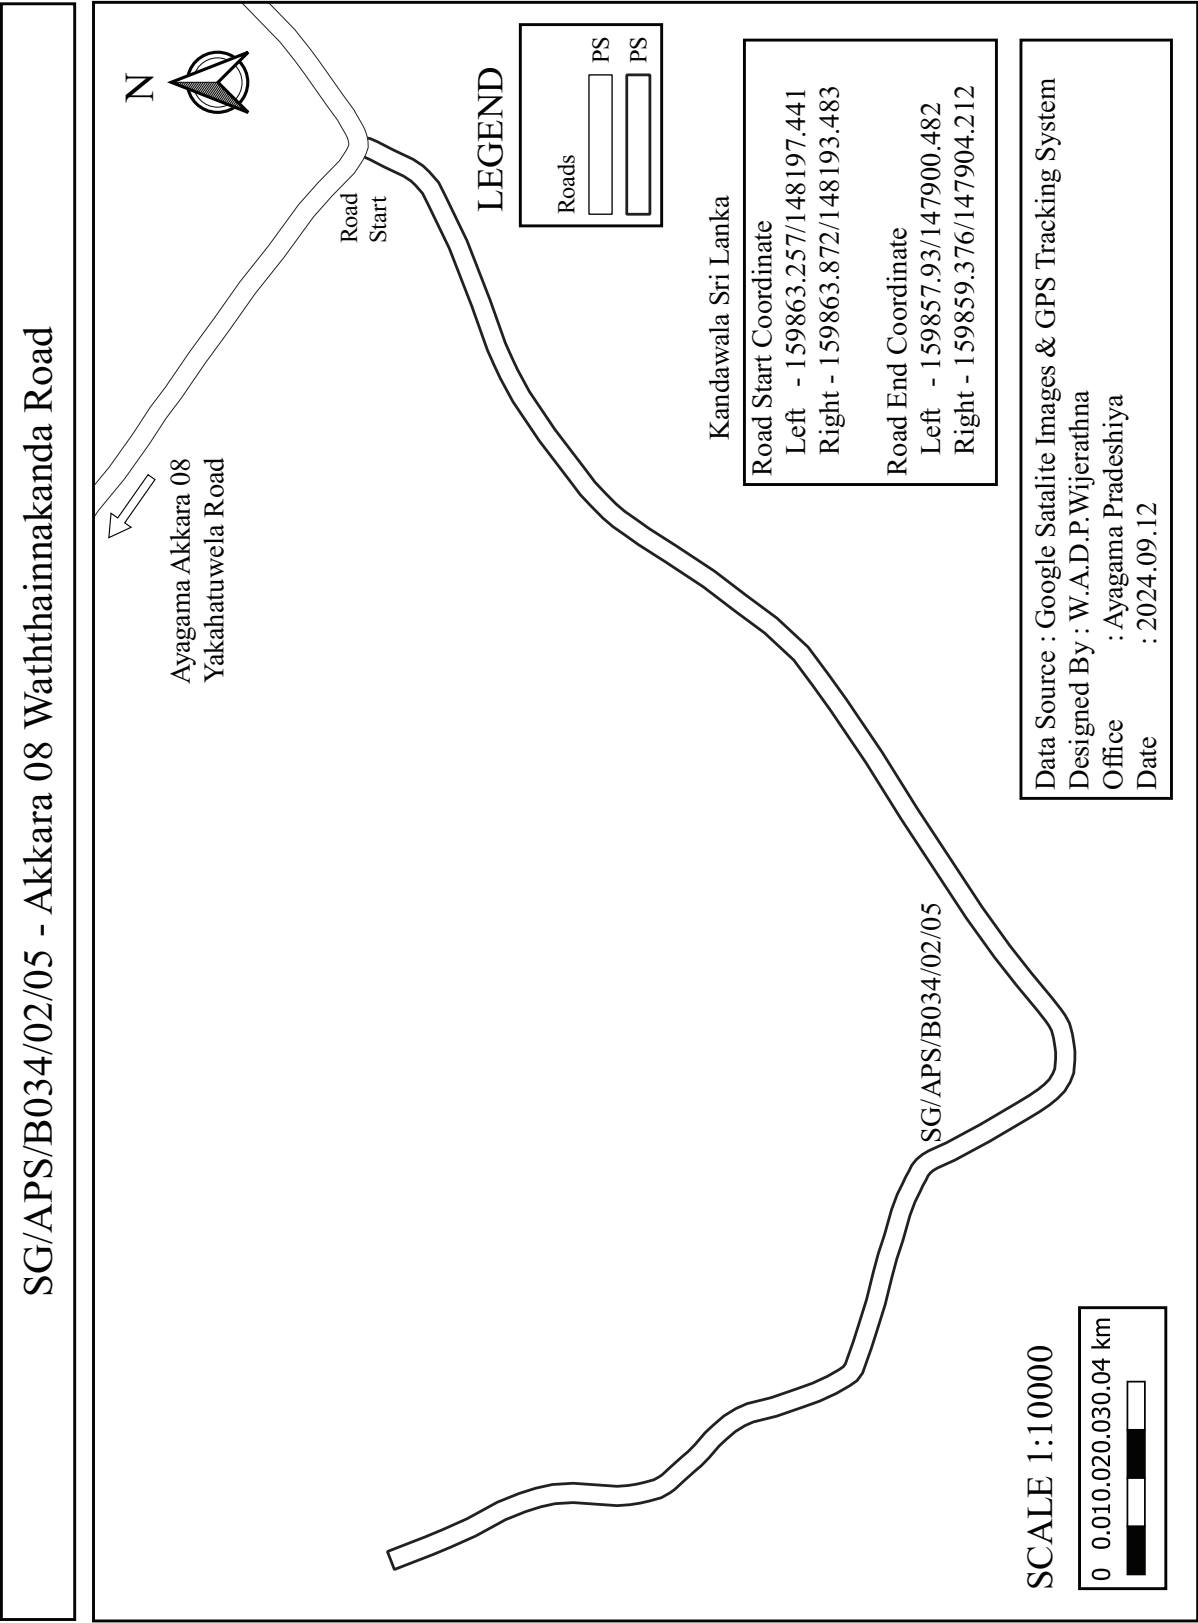

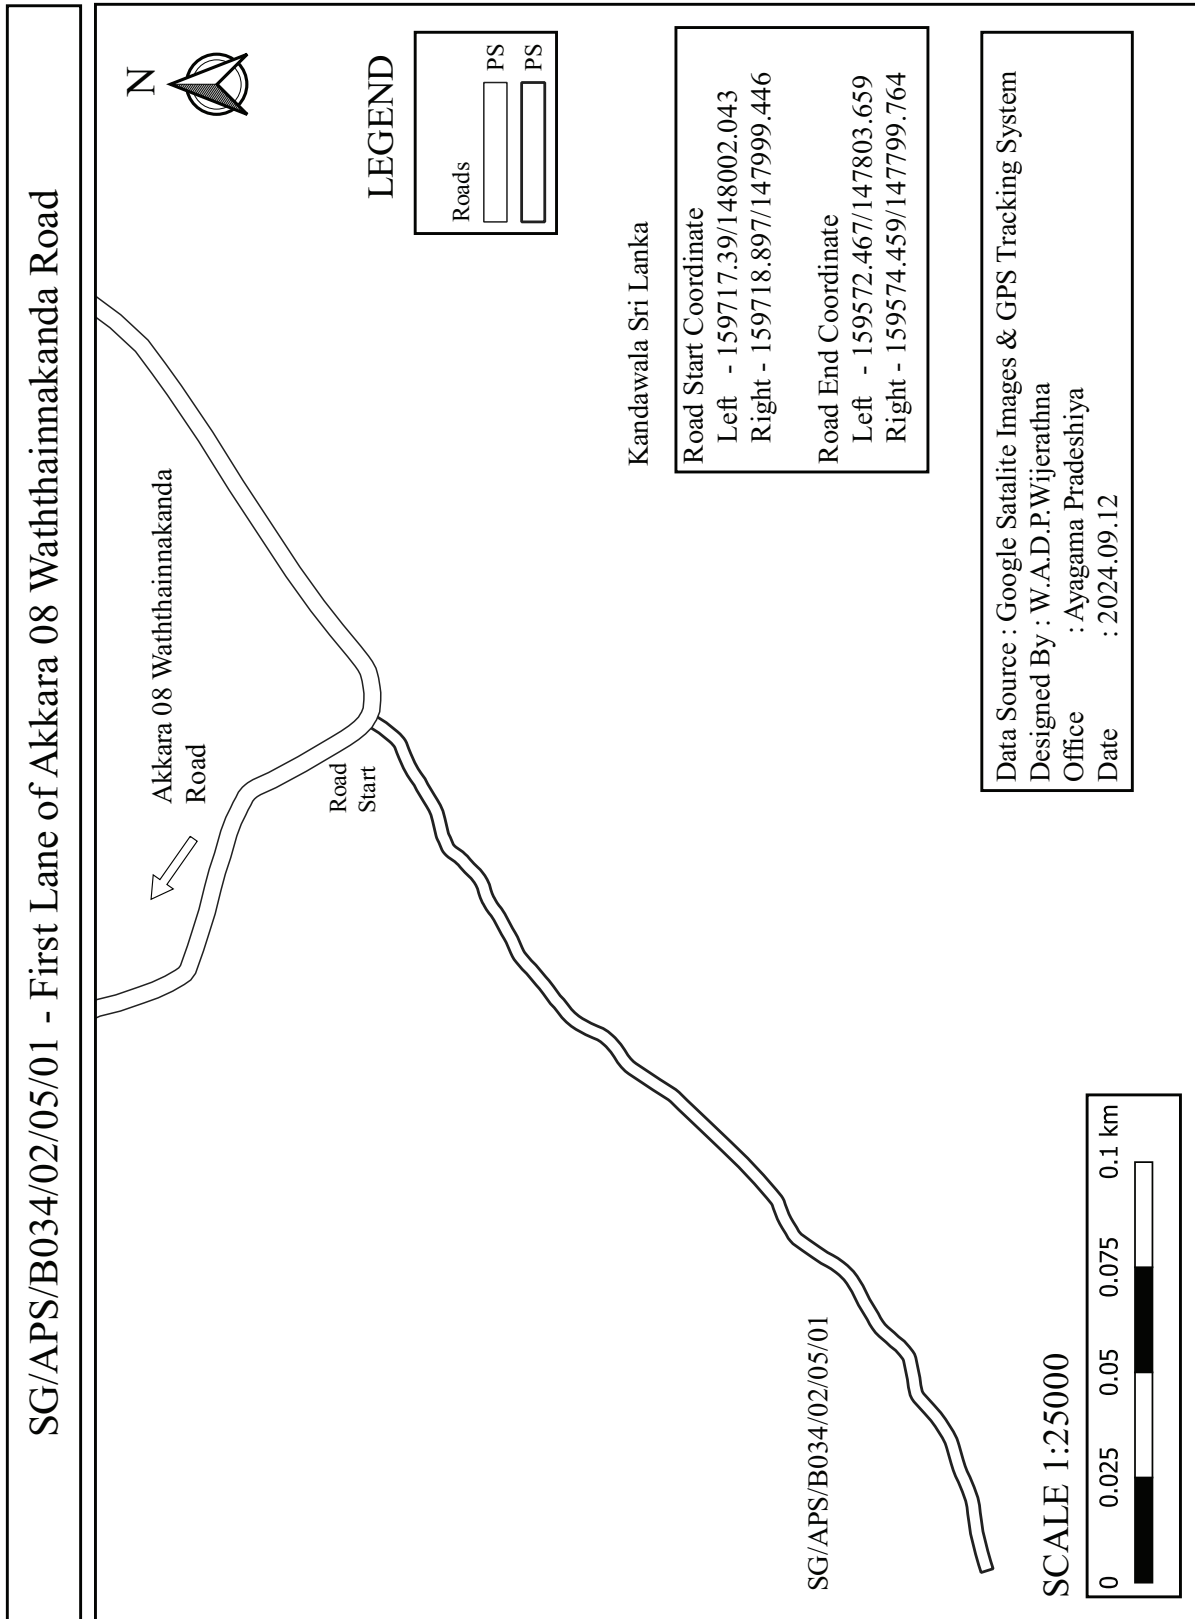

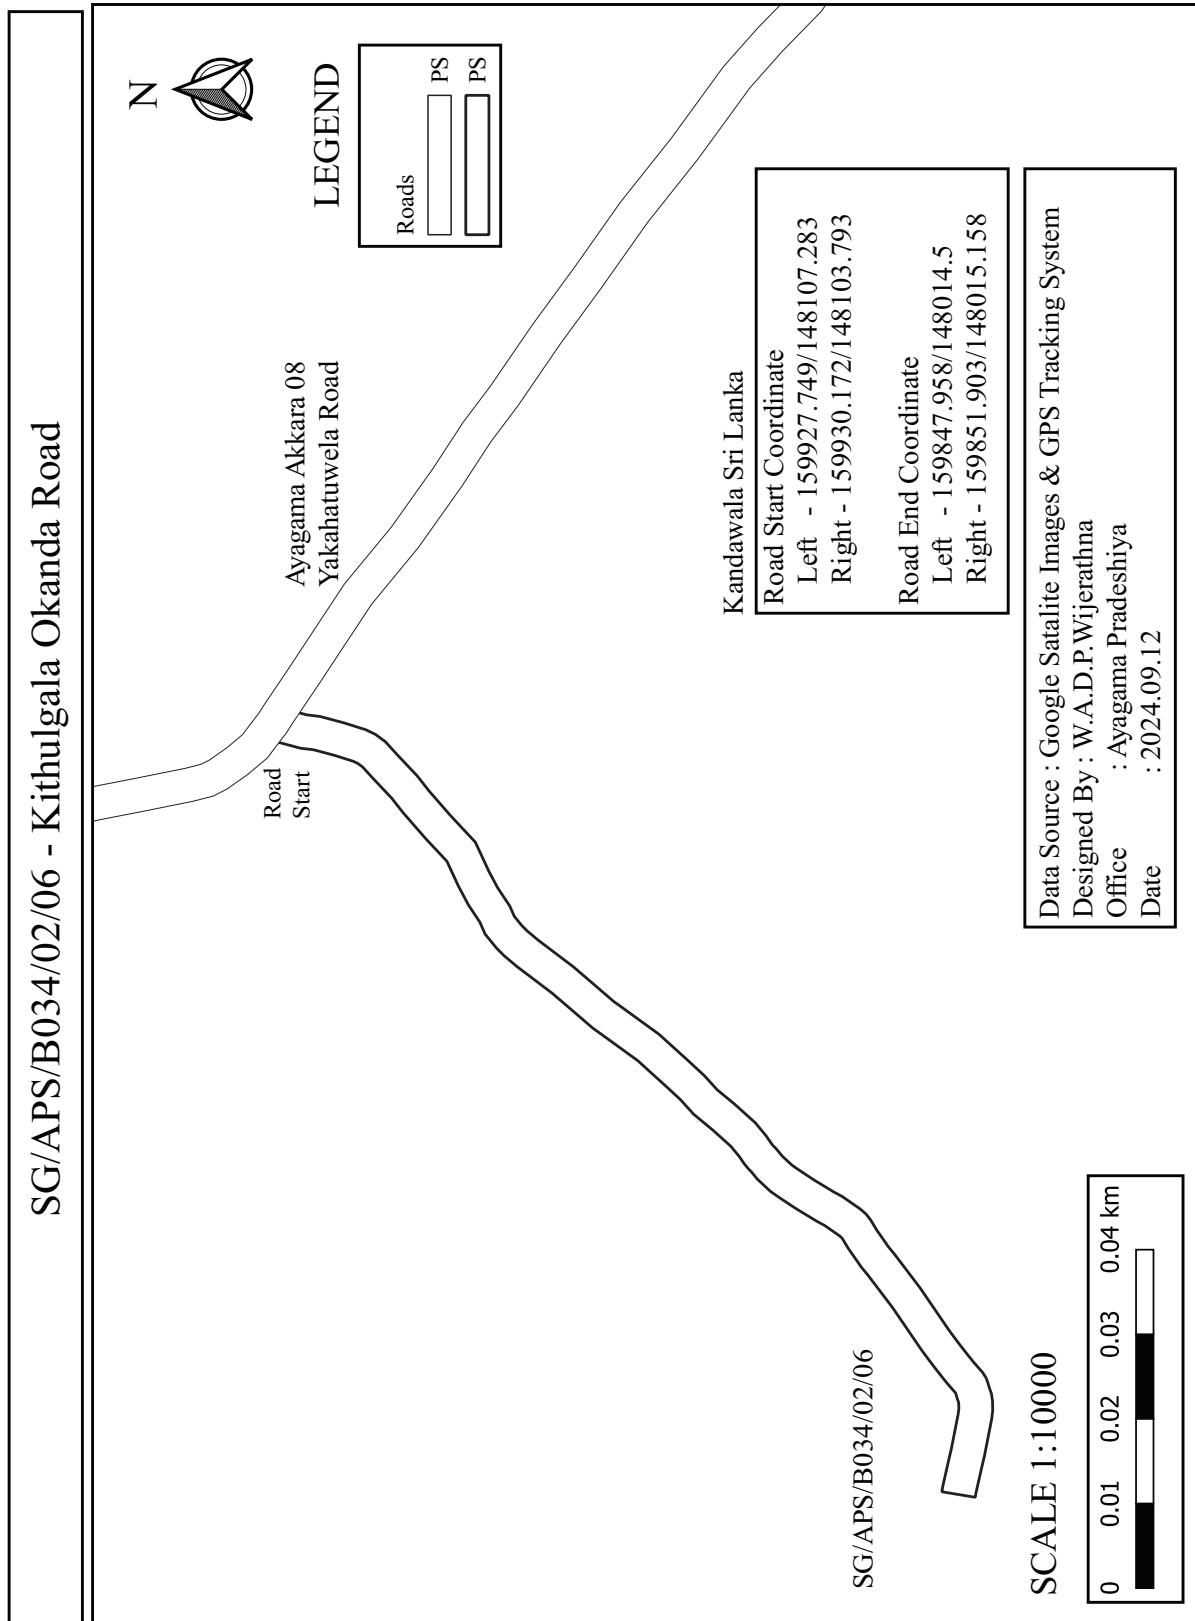

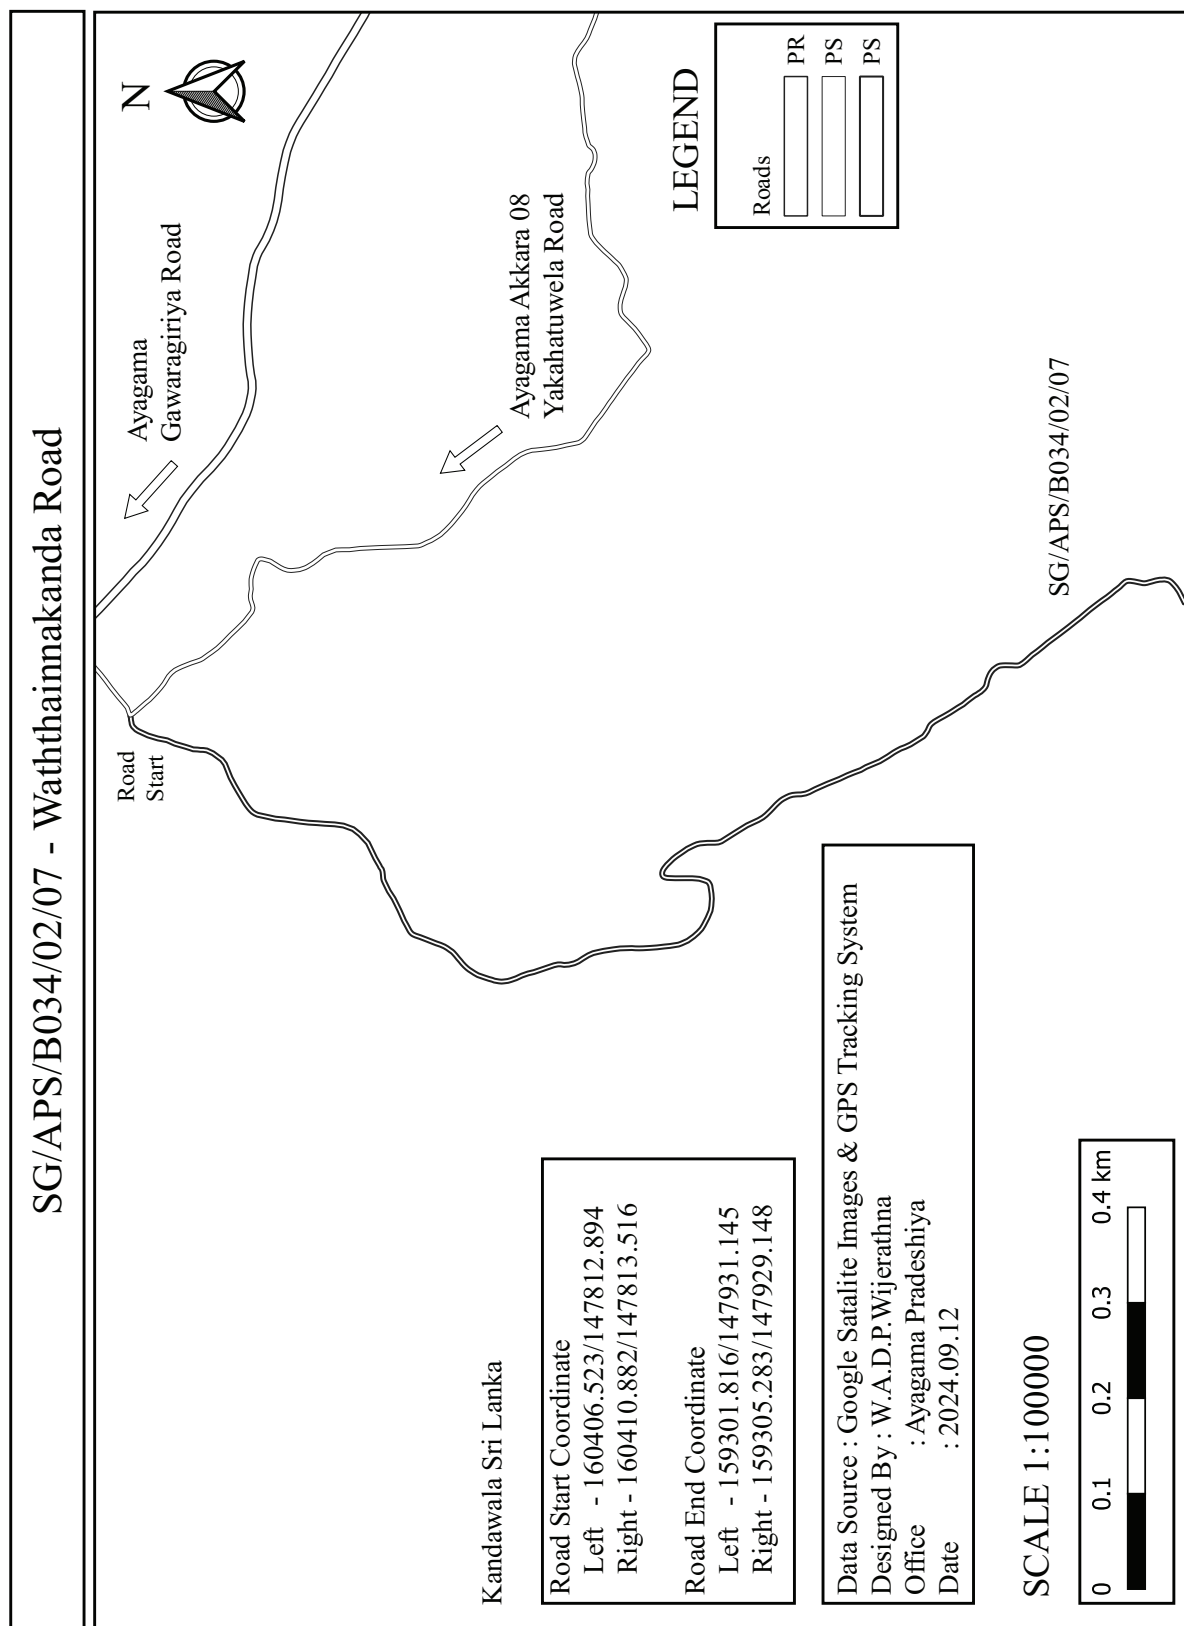

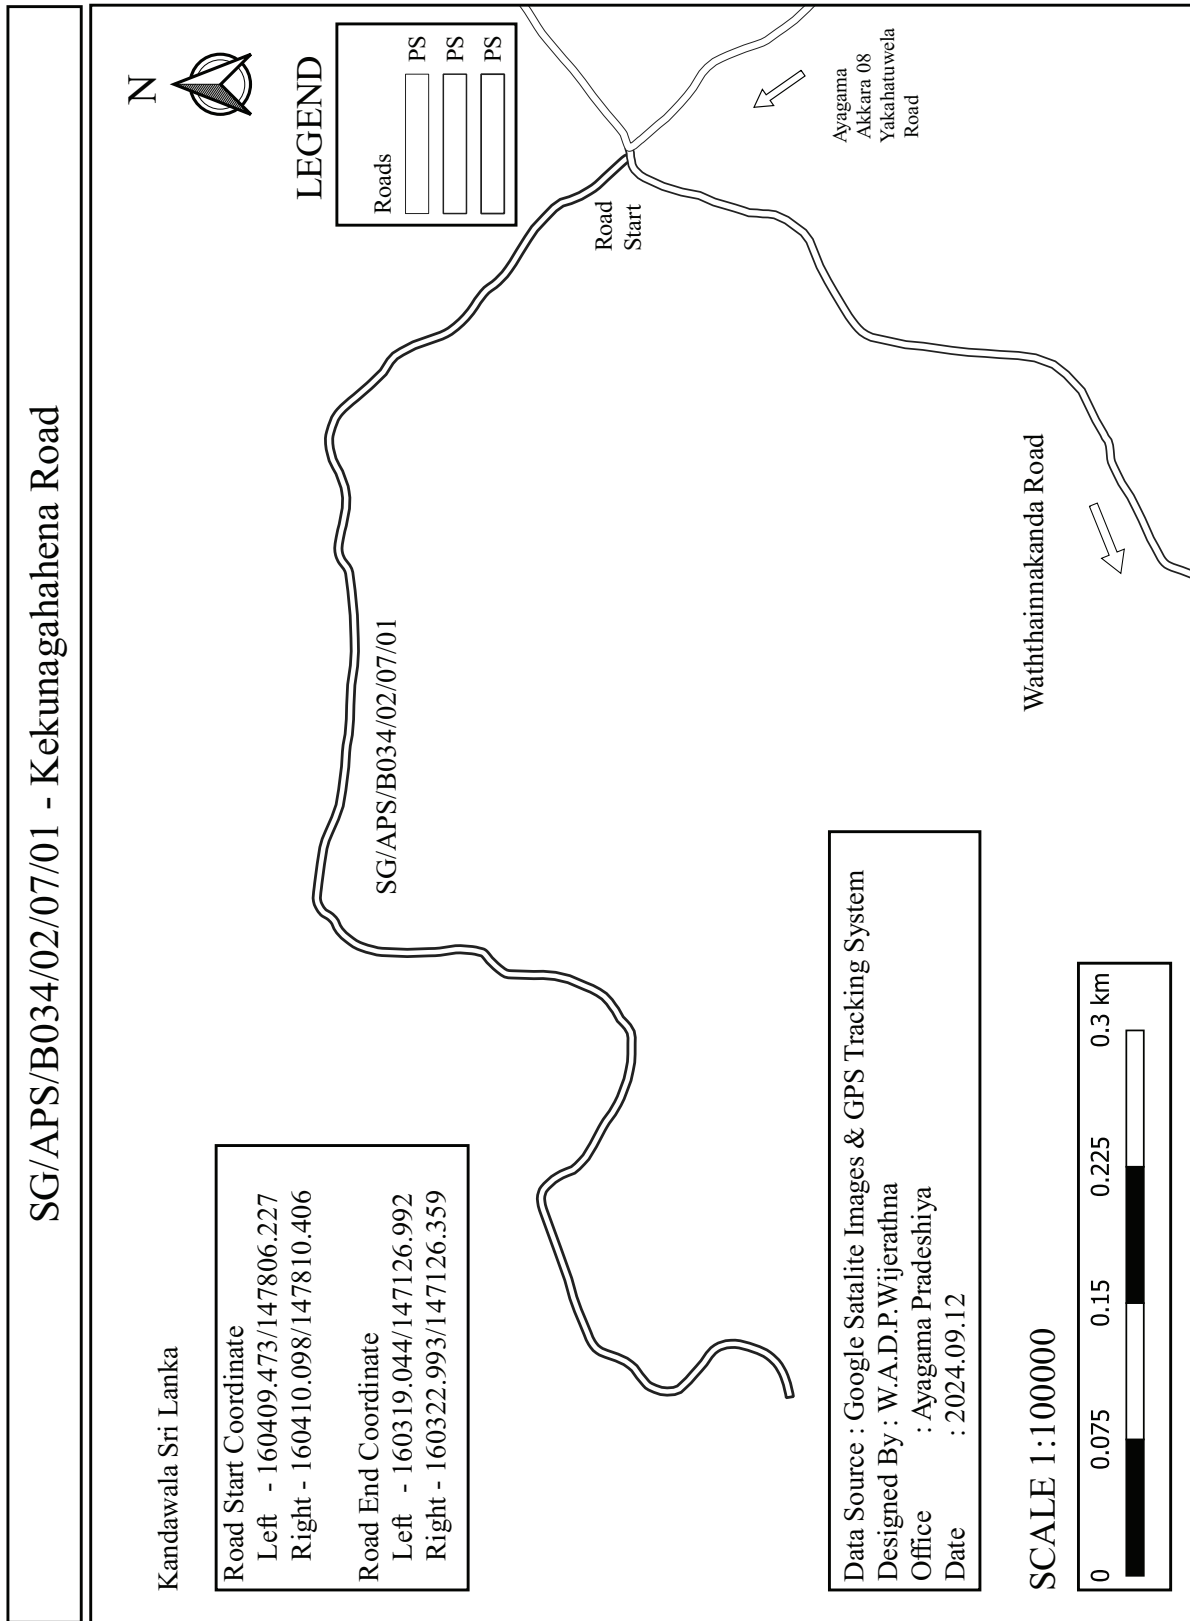

SG/APS/B034/02/07/02 - Sunimalaramaya Road



LEGEND

Roads



PS



PS

SG/APS/B034/02/07/02

Kandawala Sri Lanka

Road Start Coordinate

Left - 160275.603/147707.697

Right - 160279.735/147709.571

Road End Coordinate

Left - 1160452.02/147575.579

Right - 160454.159/147578.349

Data Source : Google Satalite Images & GPS Tracking System

Designed By : W.A.D.P.Wijerathna

Office : Ayagama Pradeshiya

Date : 2024.09.12

SCALE 1:10000

0 0.010.020.030.04 km




Waththainnakanda Road



Road Start

SG/APS/B034/02/07/03 - First Lane of Waththainnakanda Road

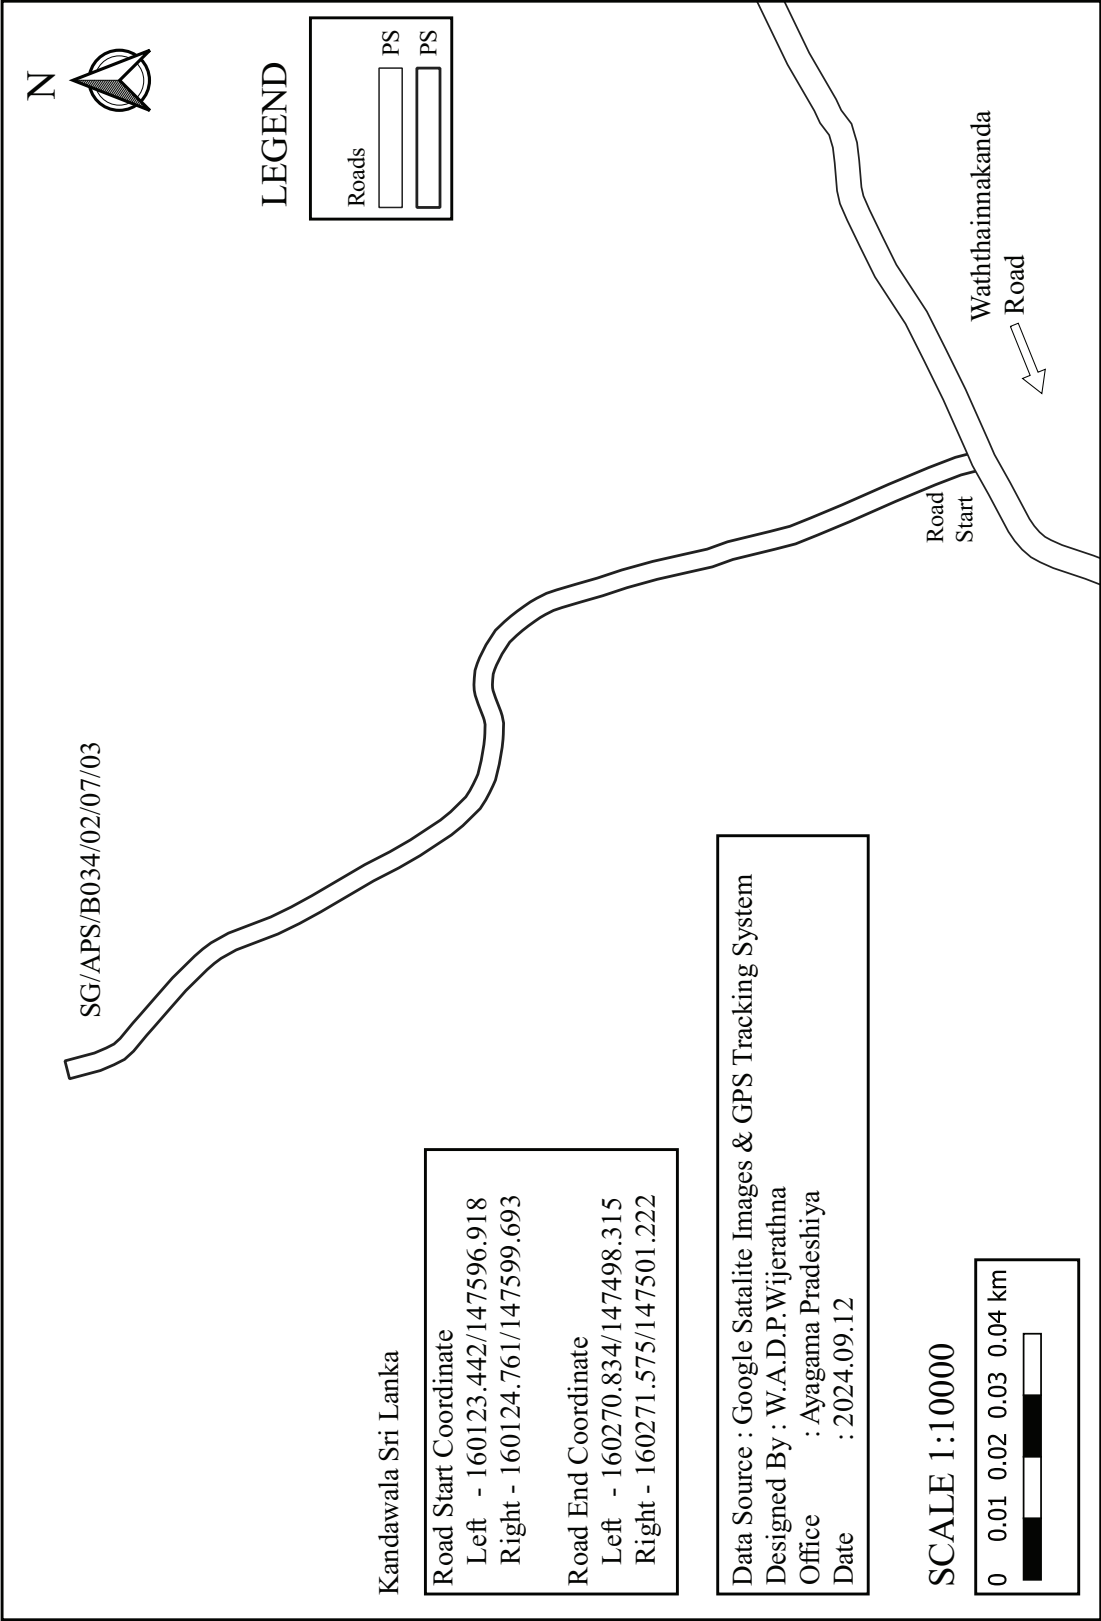

SG/APS/B034/02/07/04 - Malwela Sub Footpath



SG/APS/B034/02/07/04

Road Start

LEGEND

Roads

PS

PS

Wathhainnakanda Road

Kandawala Sri Lanka

Road Start Coordinate

Left - 160115.296/147583.669

Right - 160117.421/147586.06

Road End Coordinate

Left - 160080.563/147501.059

Right - 160083.058/147499.39

Data Source : Google Satalite Images & GPS Tracking System


Designed By : W.A.D.P.Wijerathna


Office : Ayagama Pradeshiya


Date : 2024.09.12


SCALE 1:10000




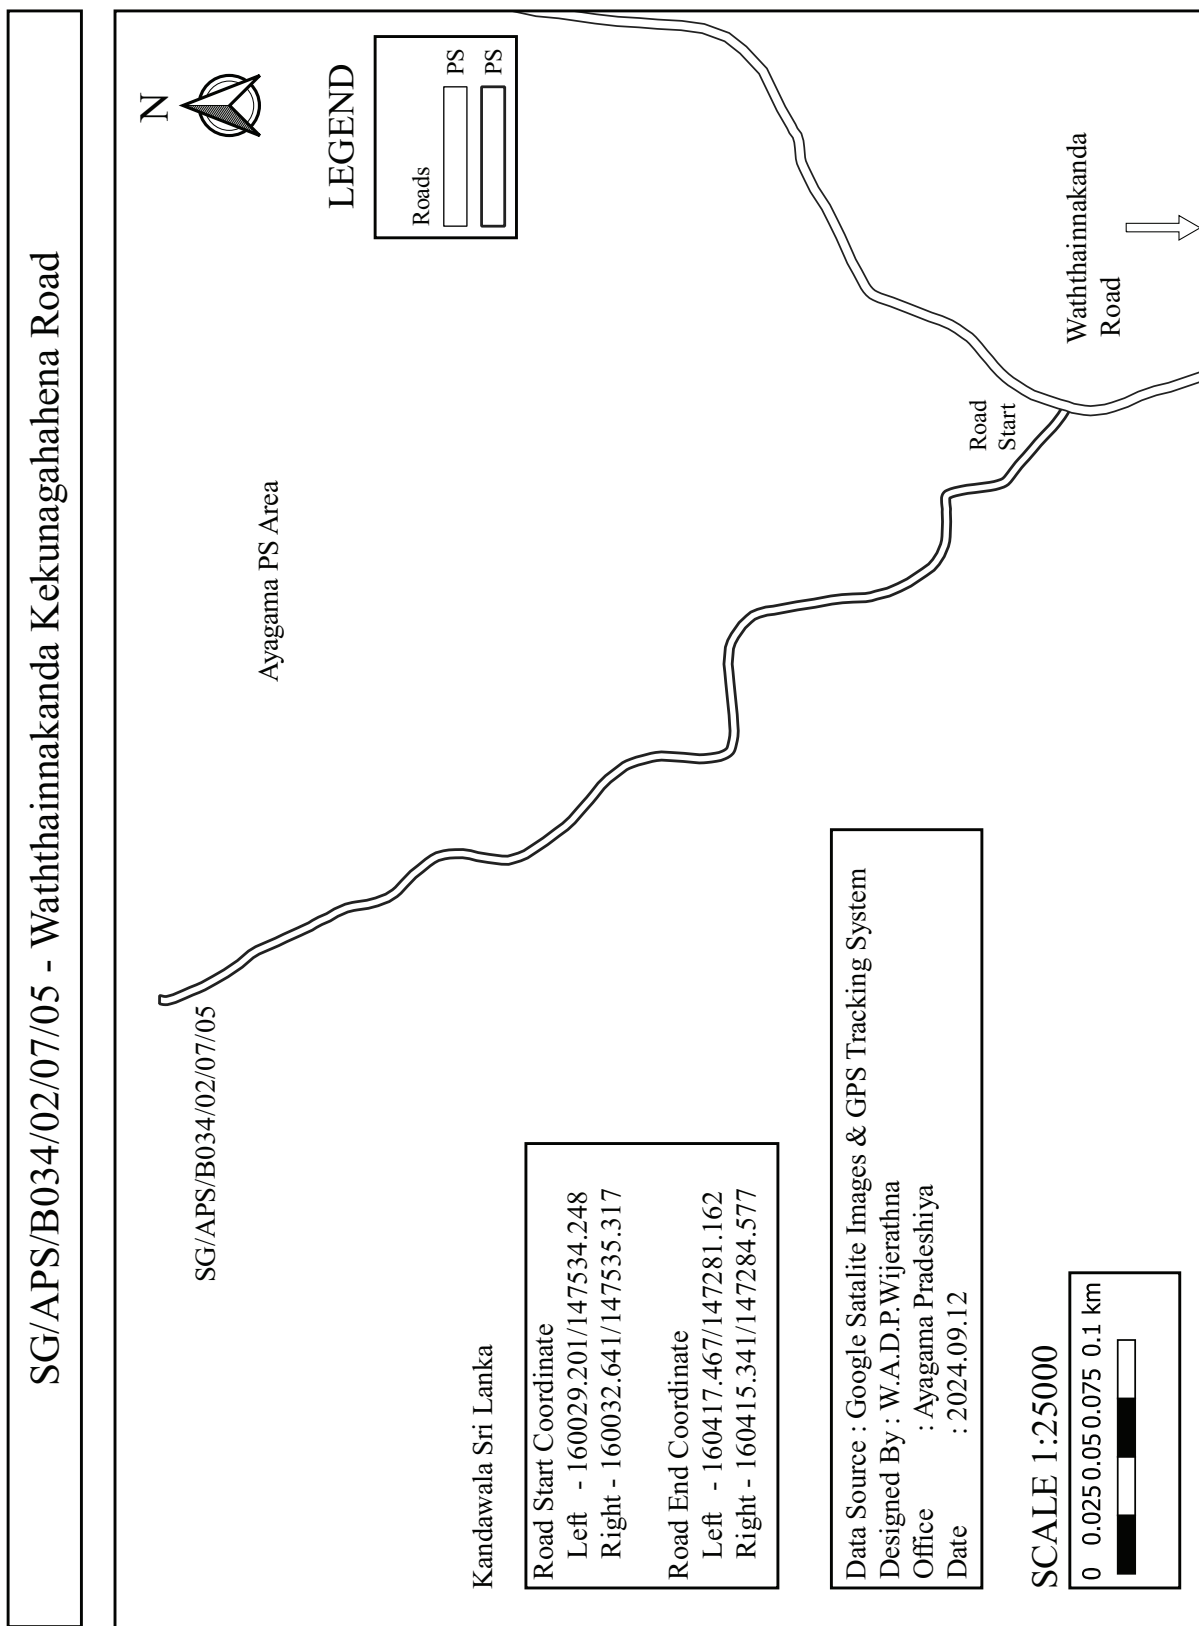


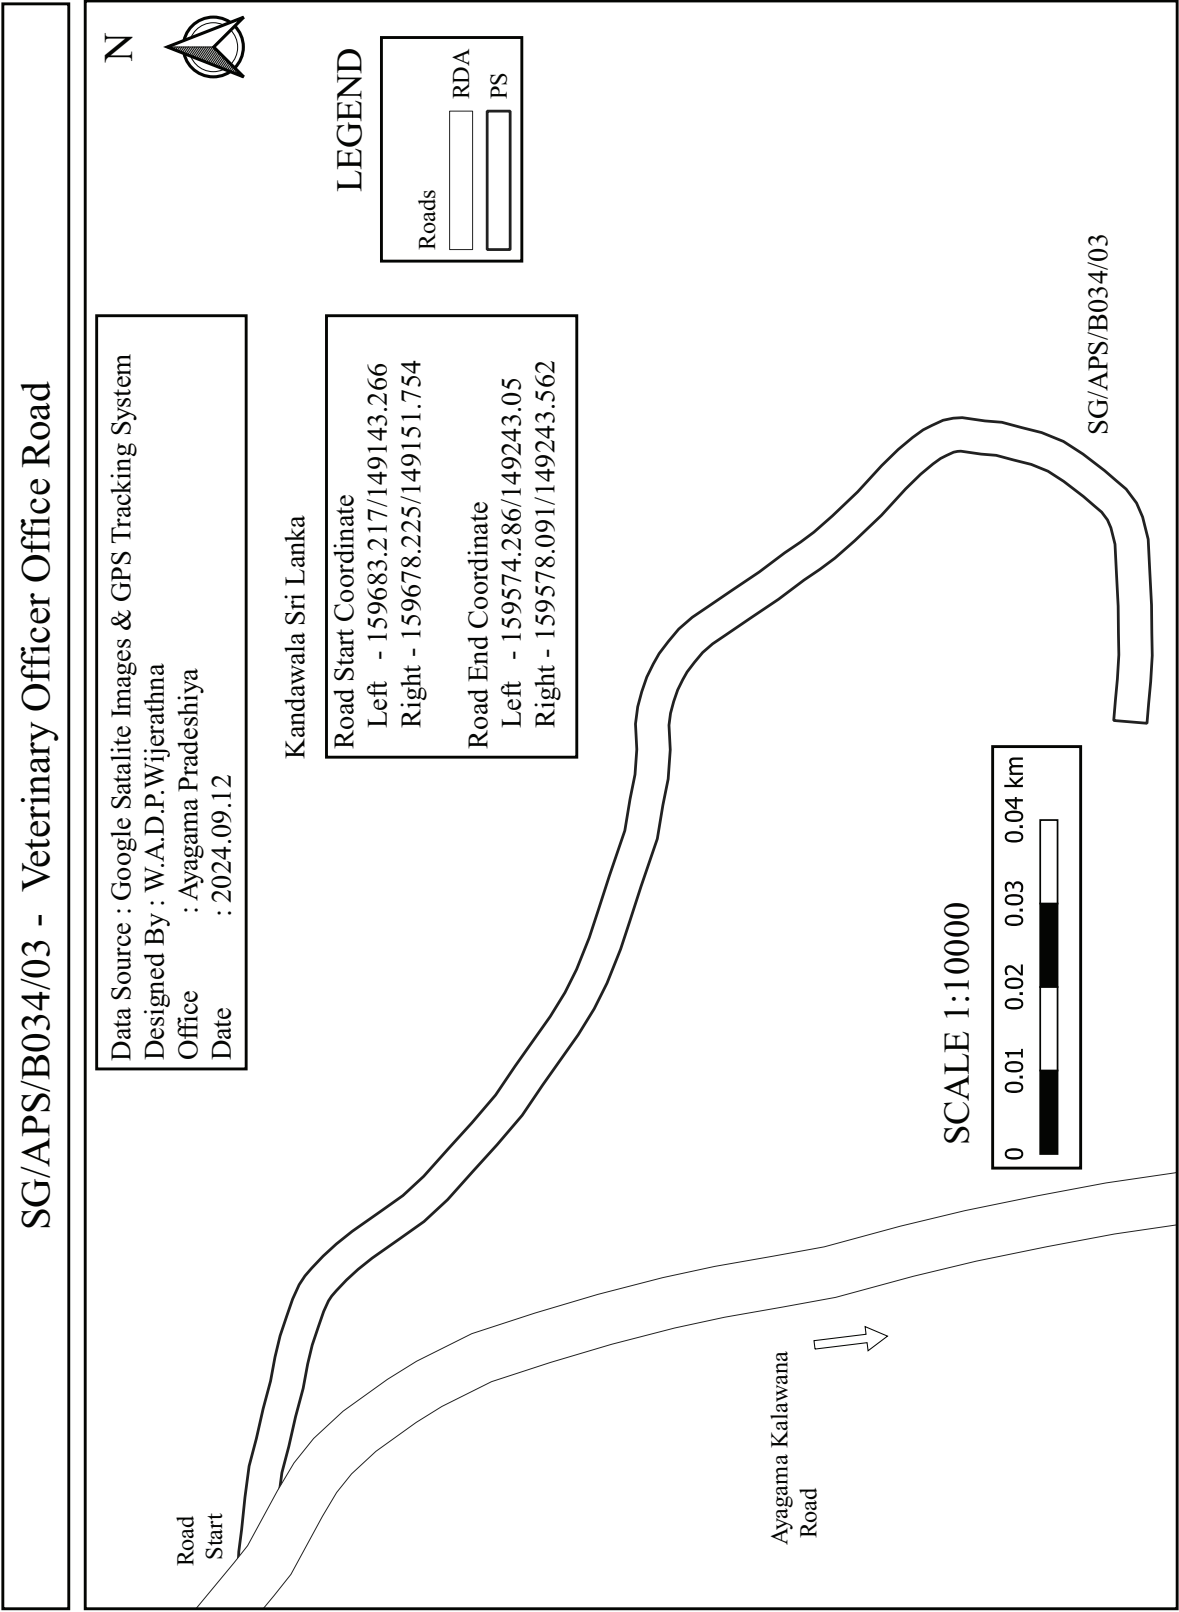


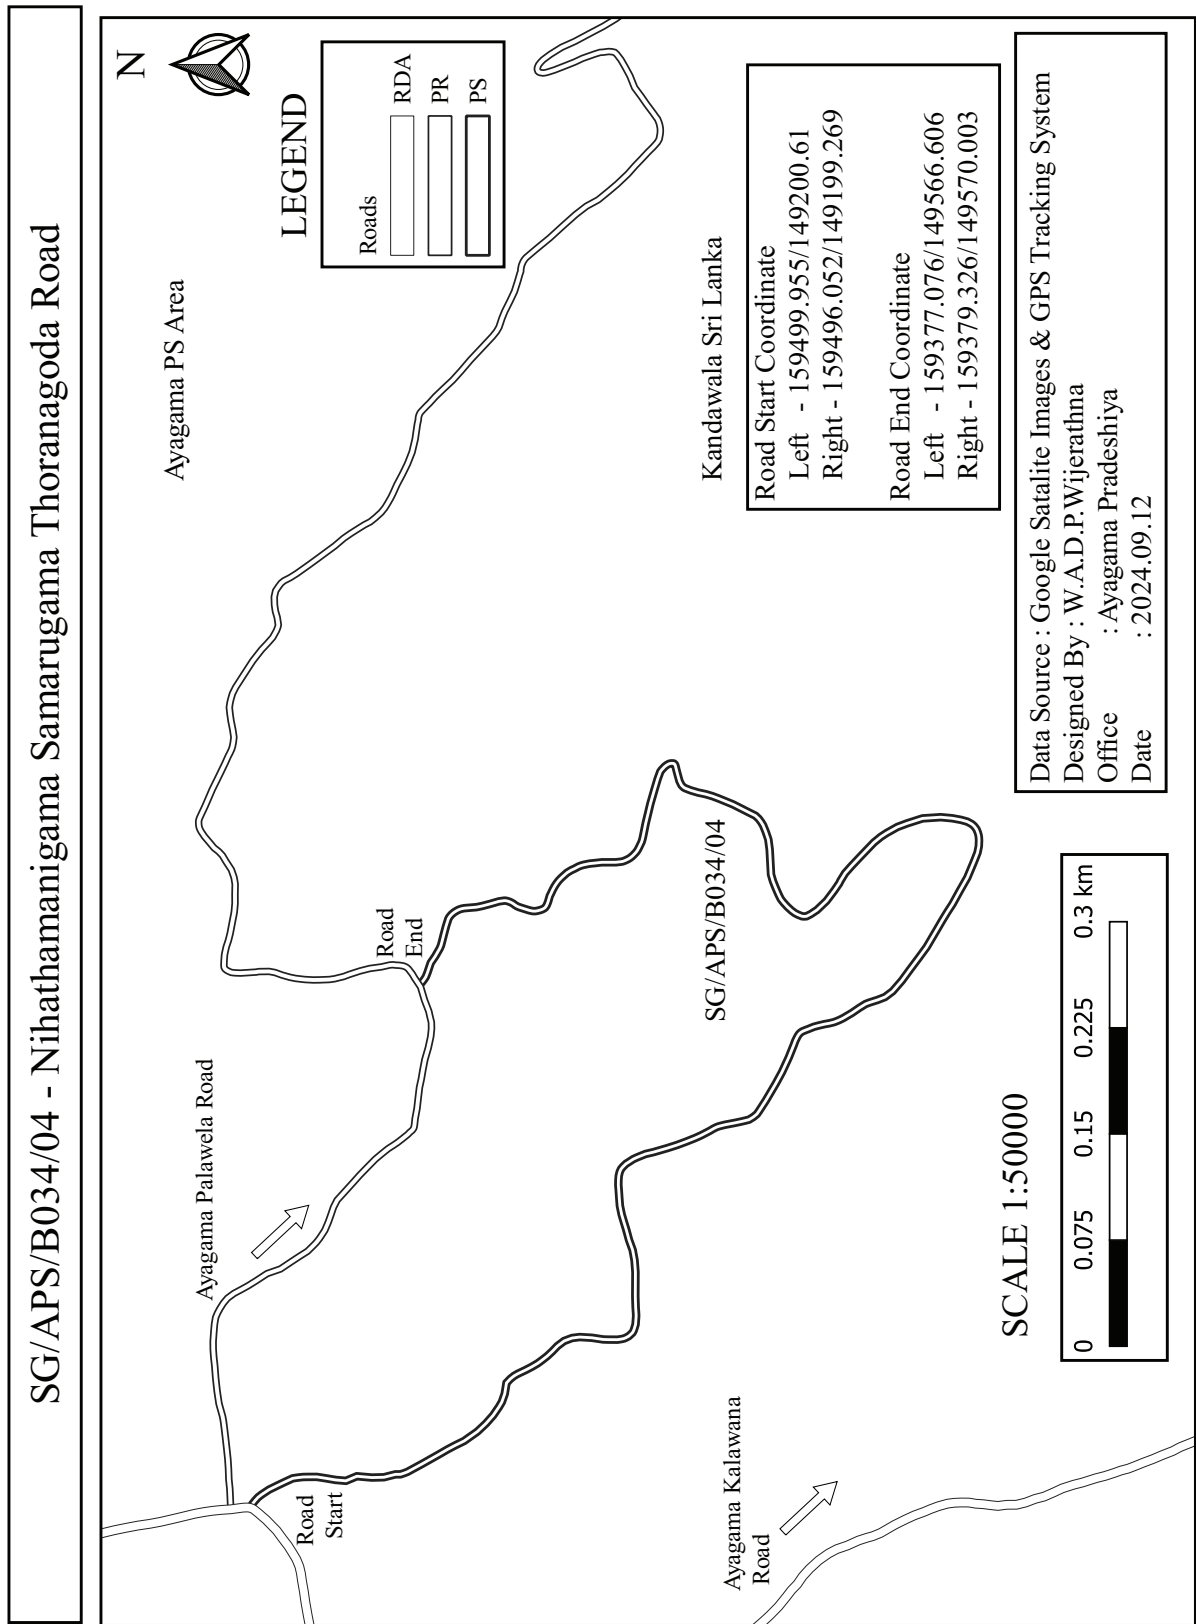


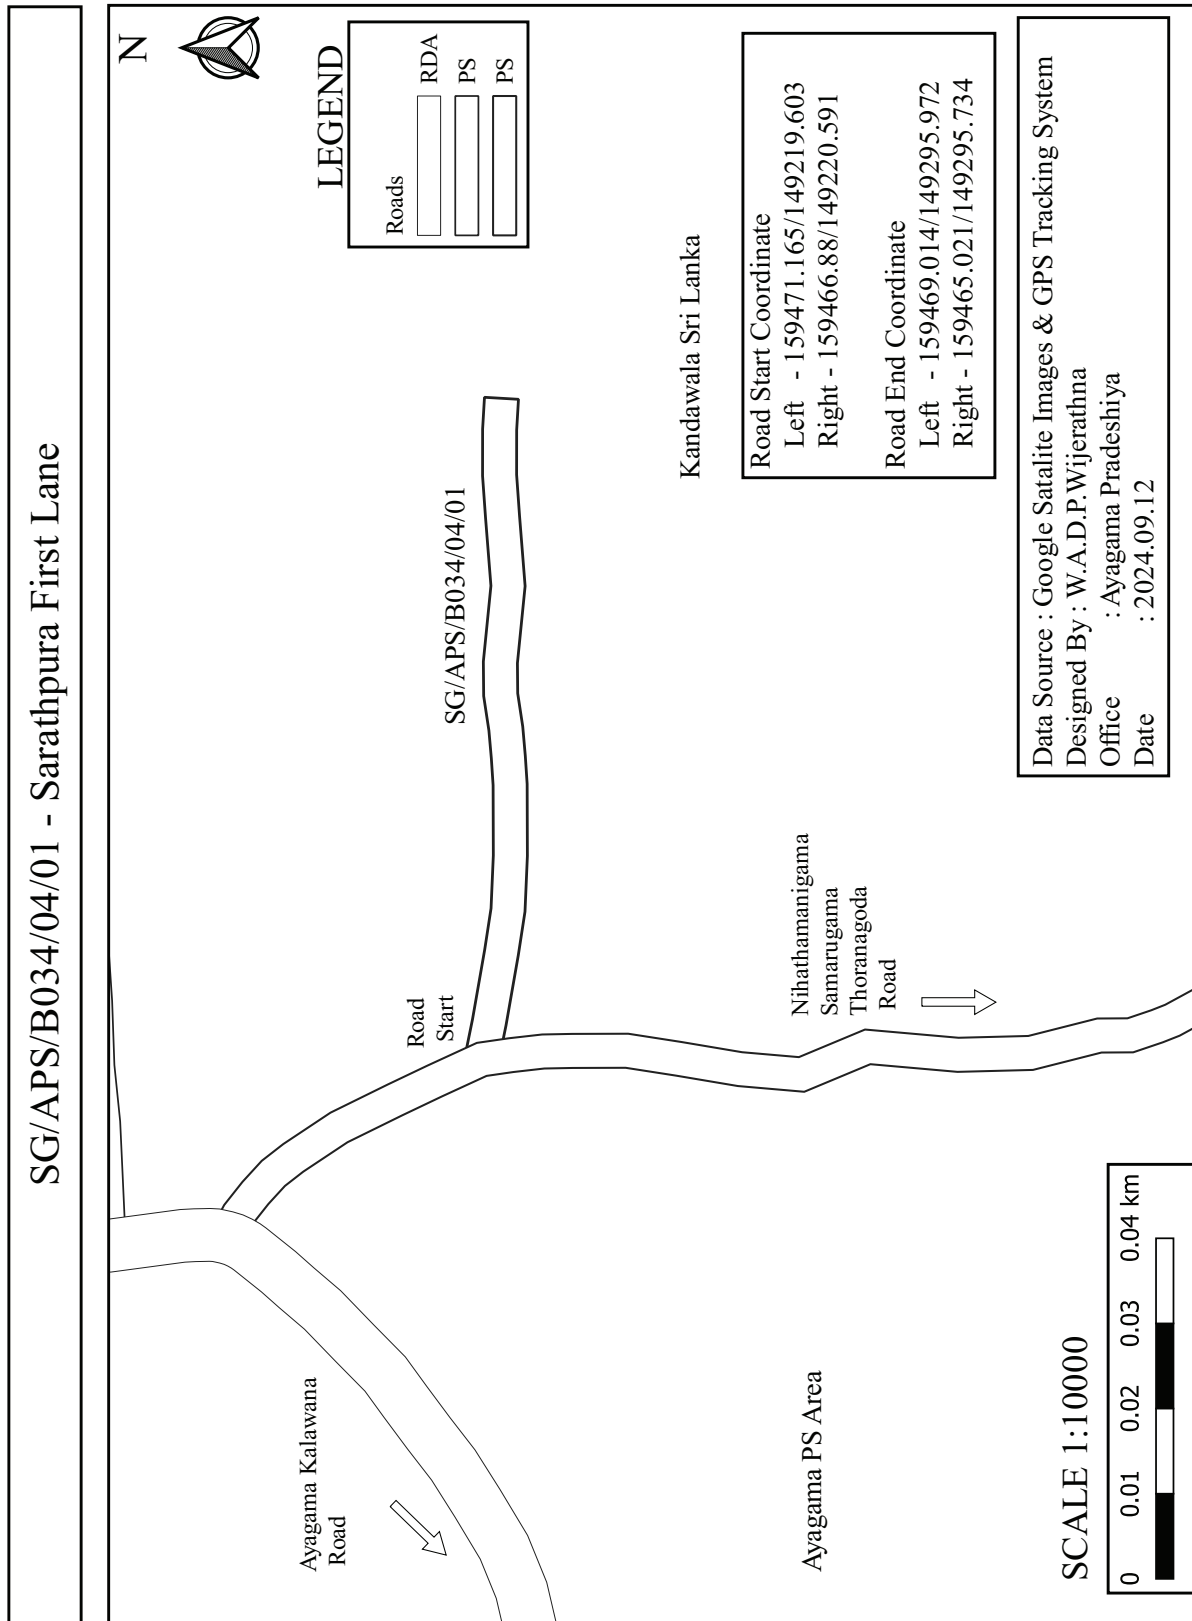


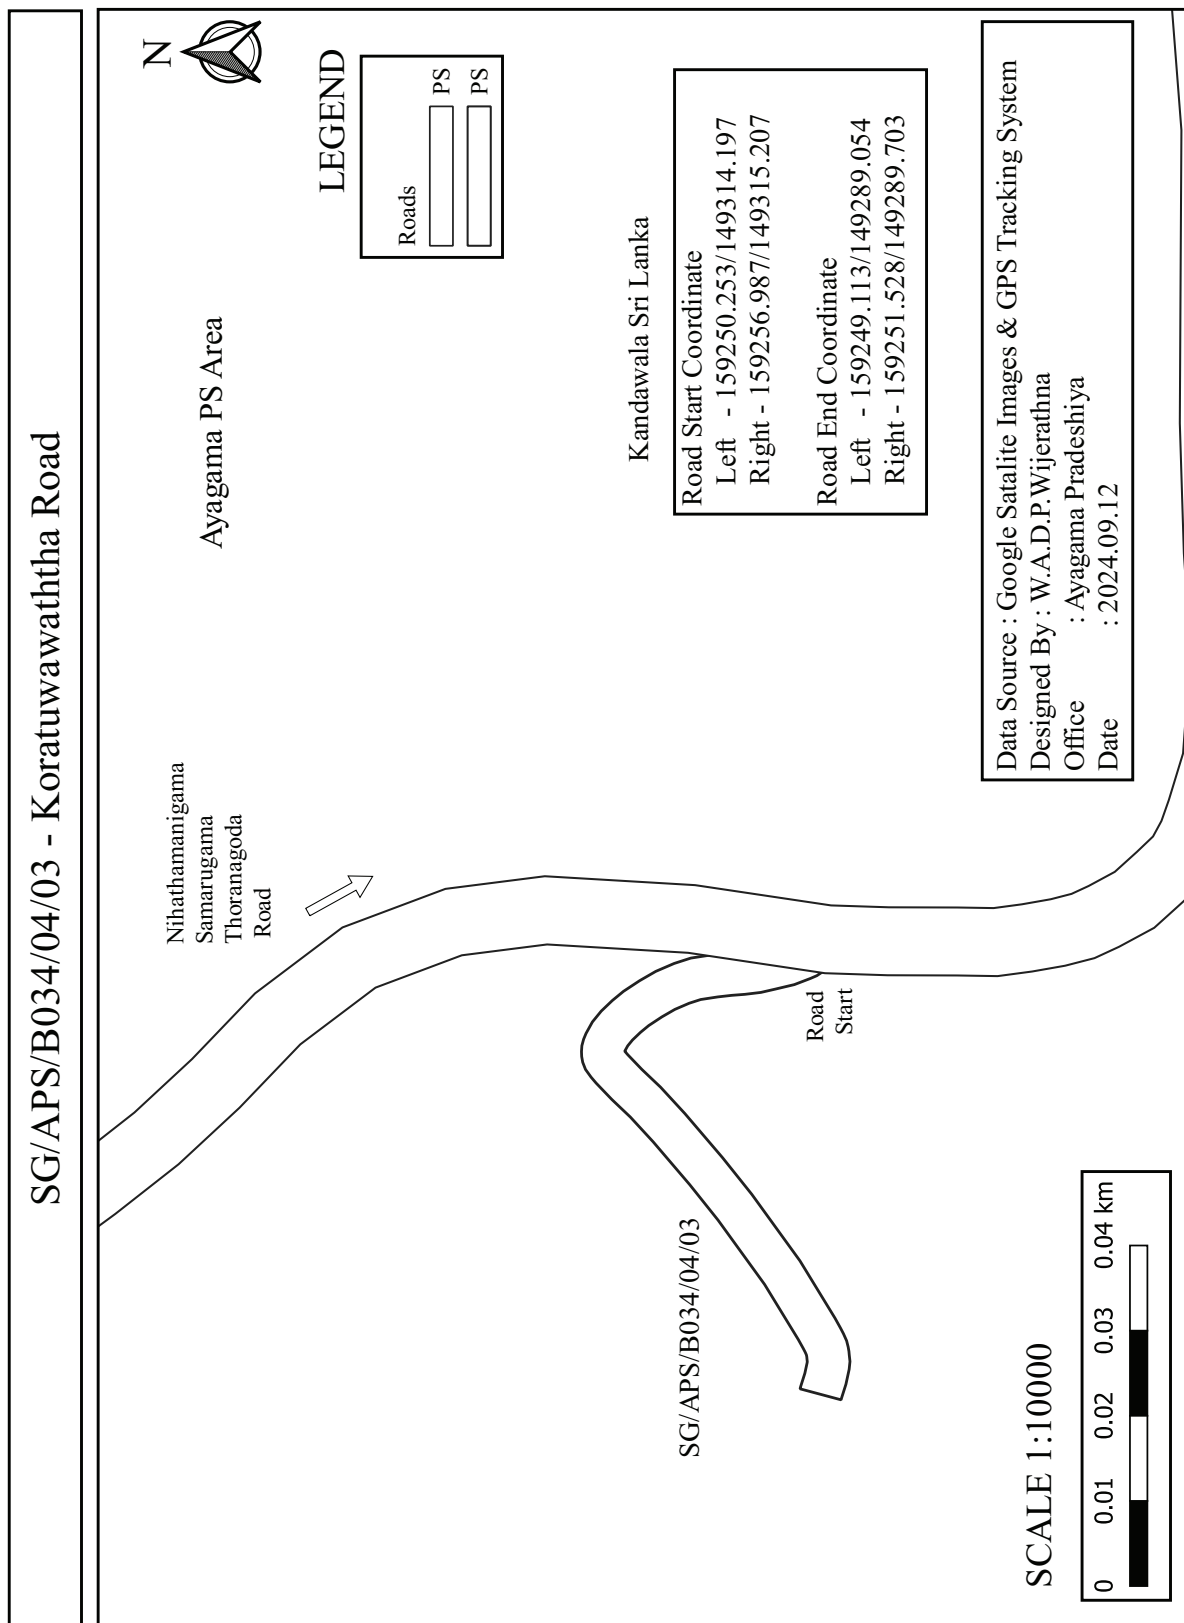


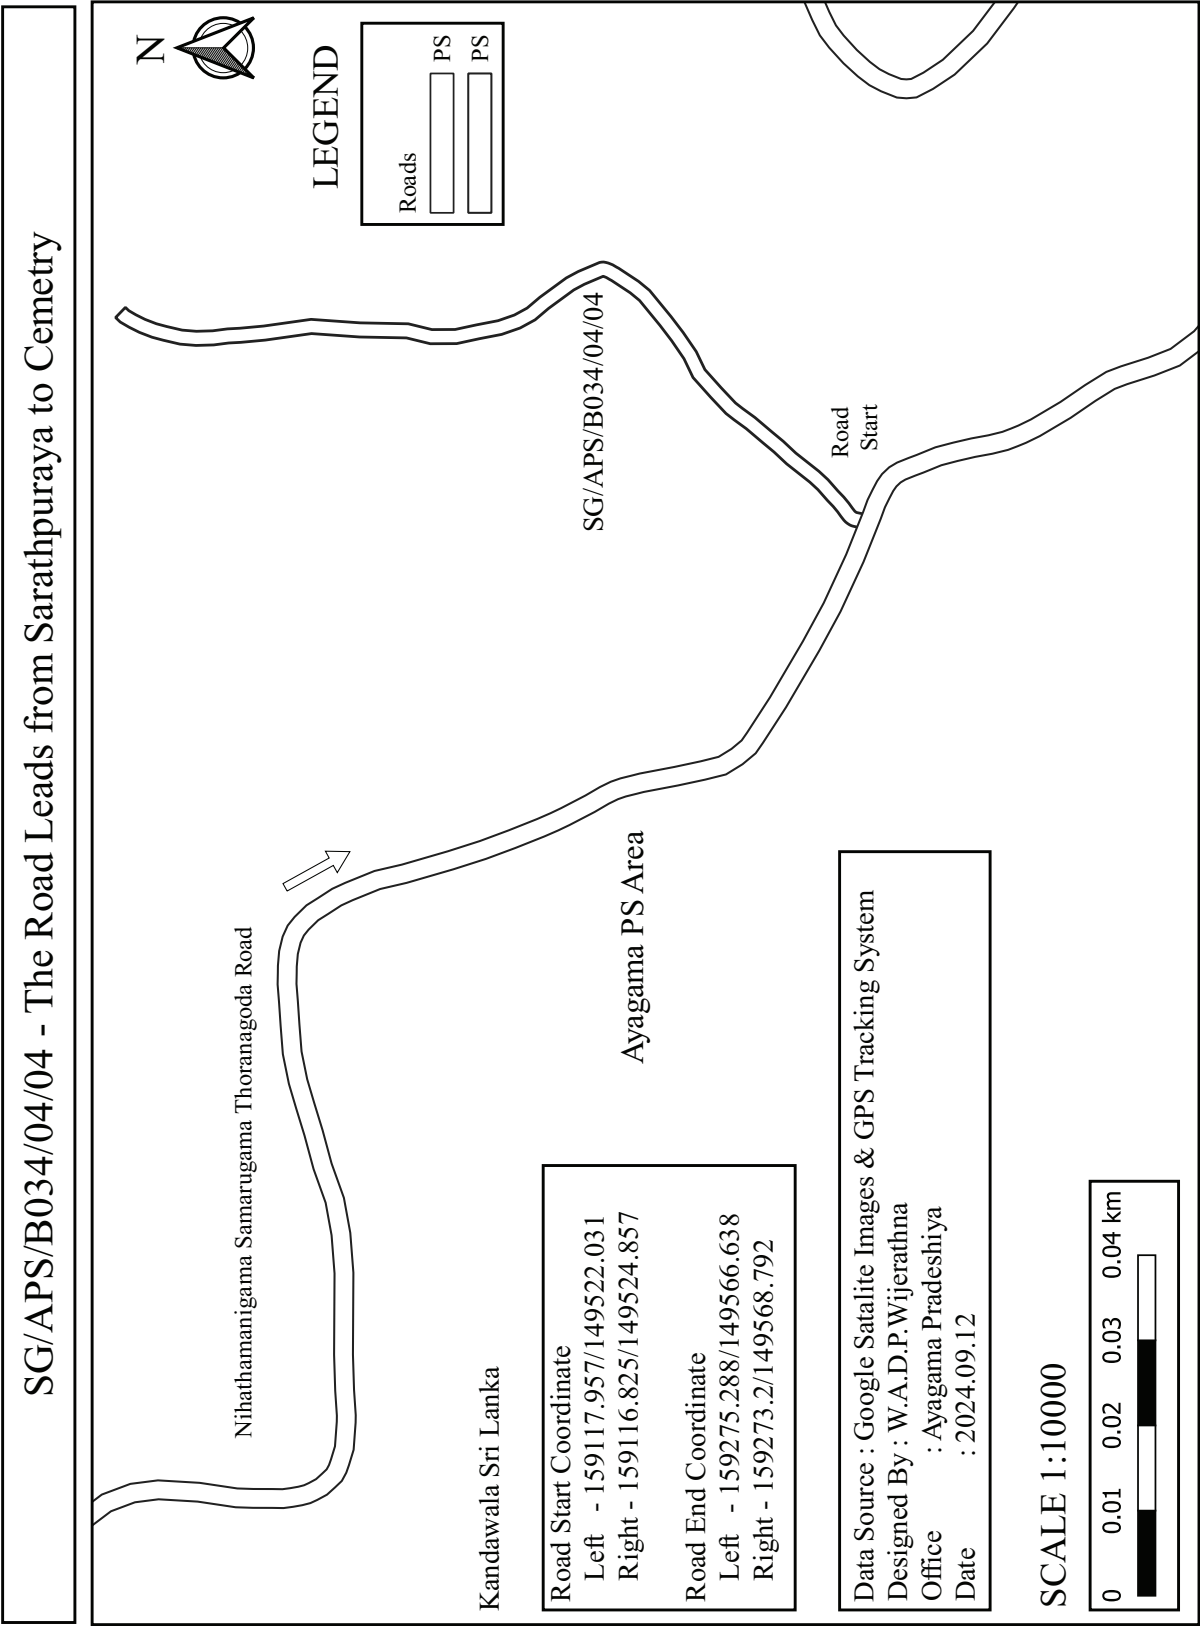


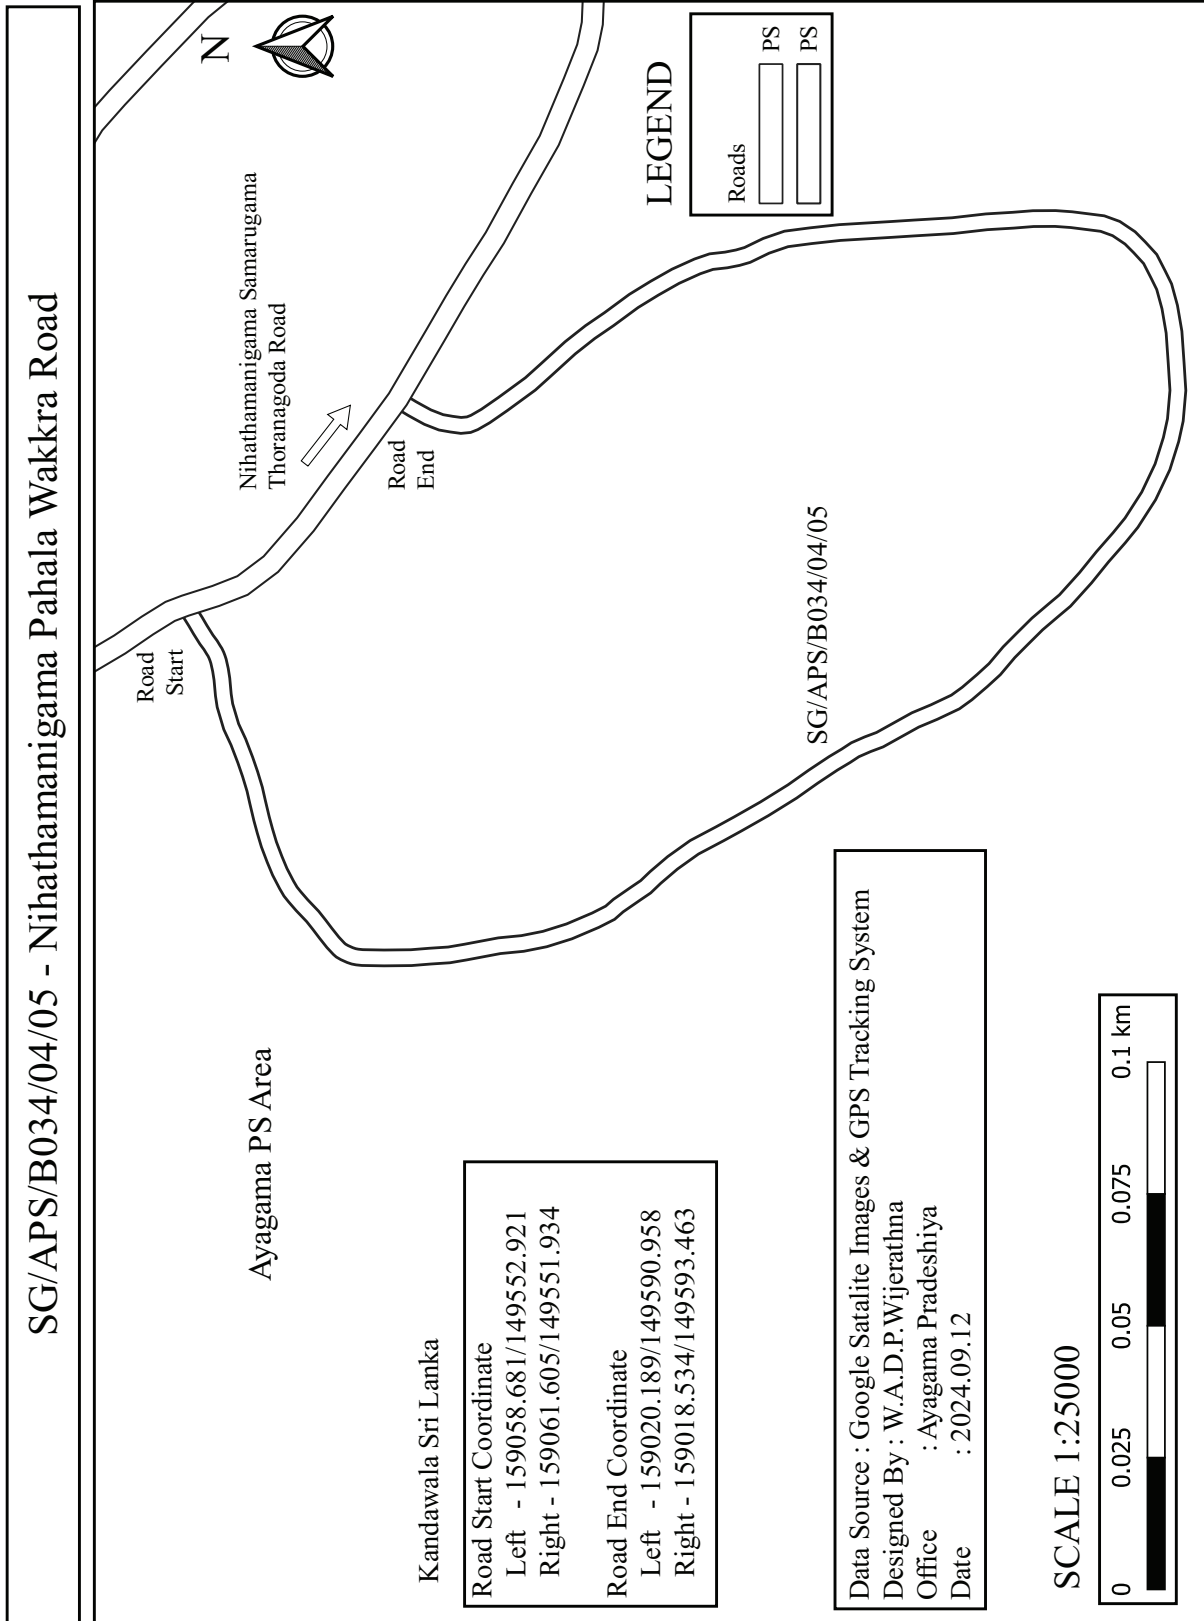


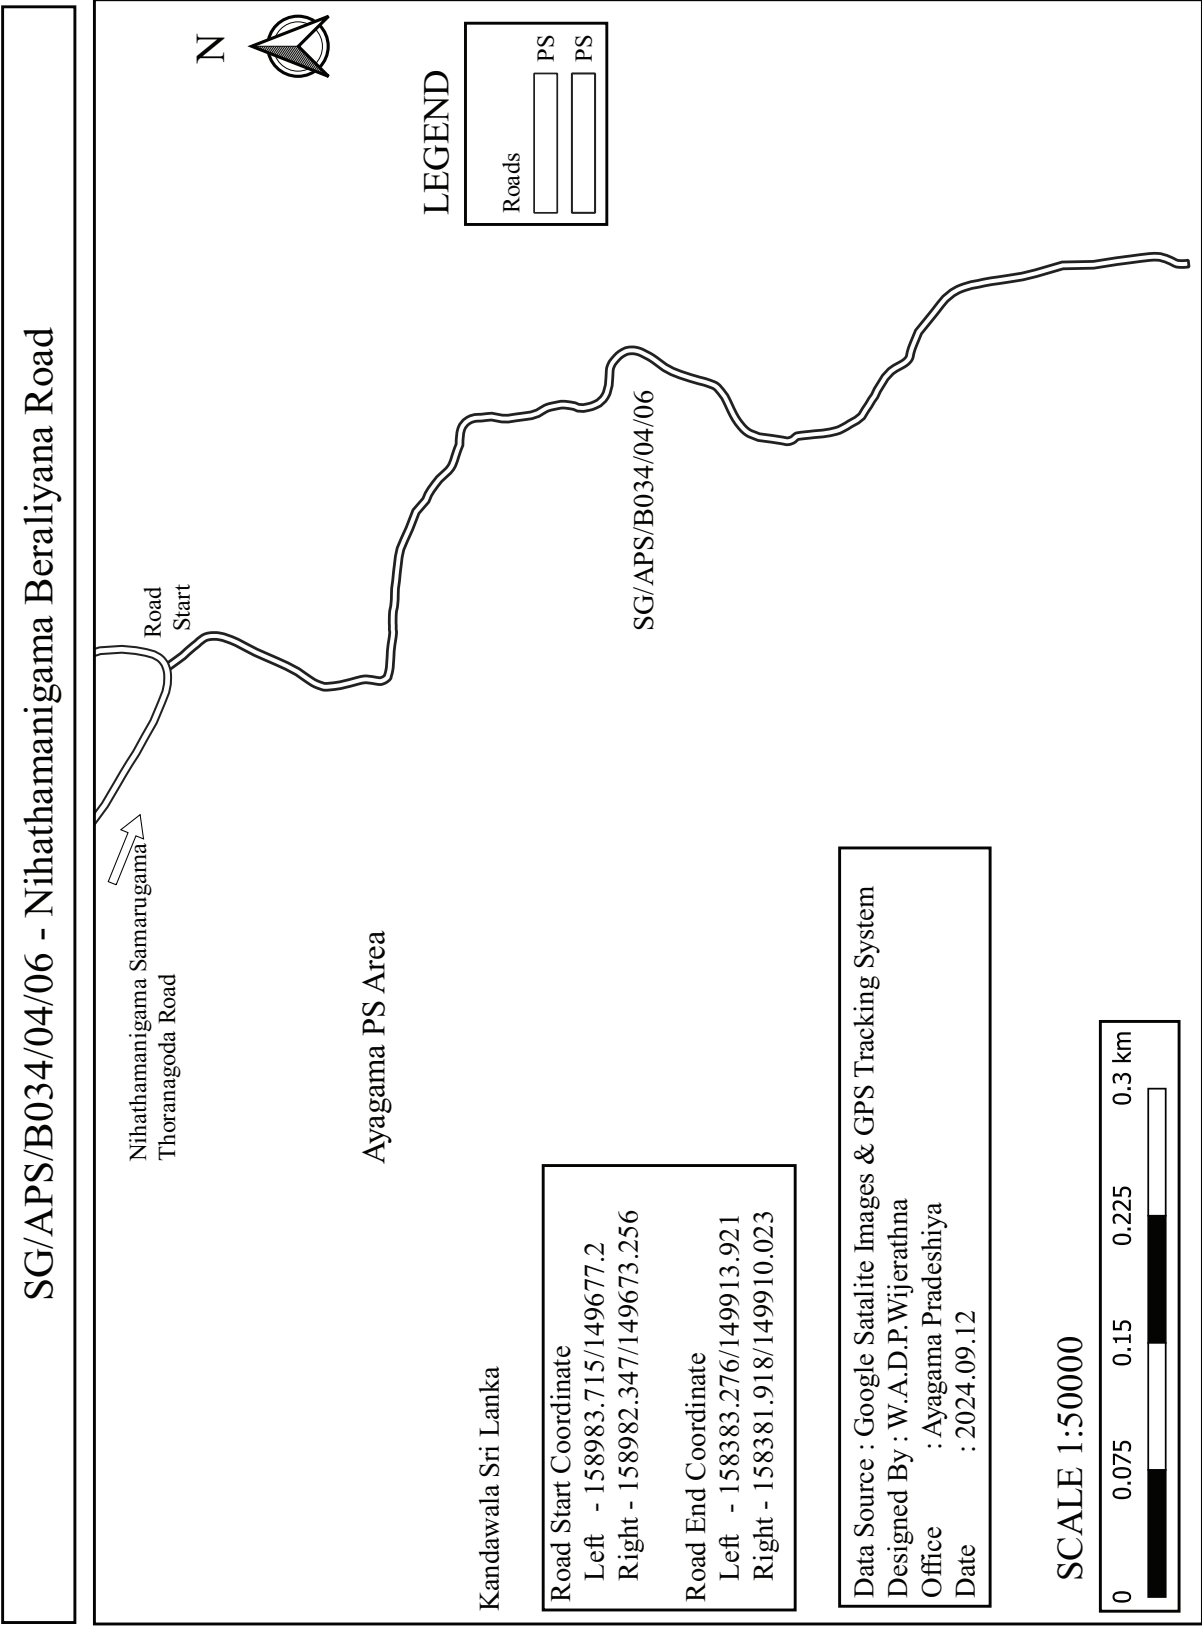


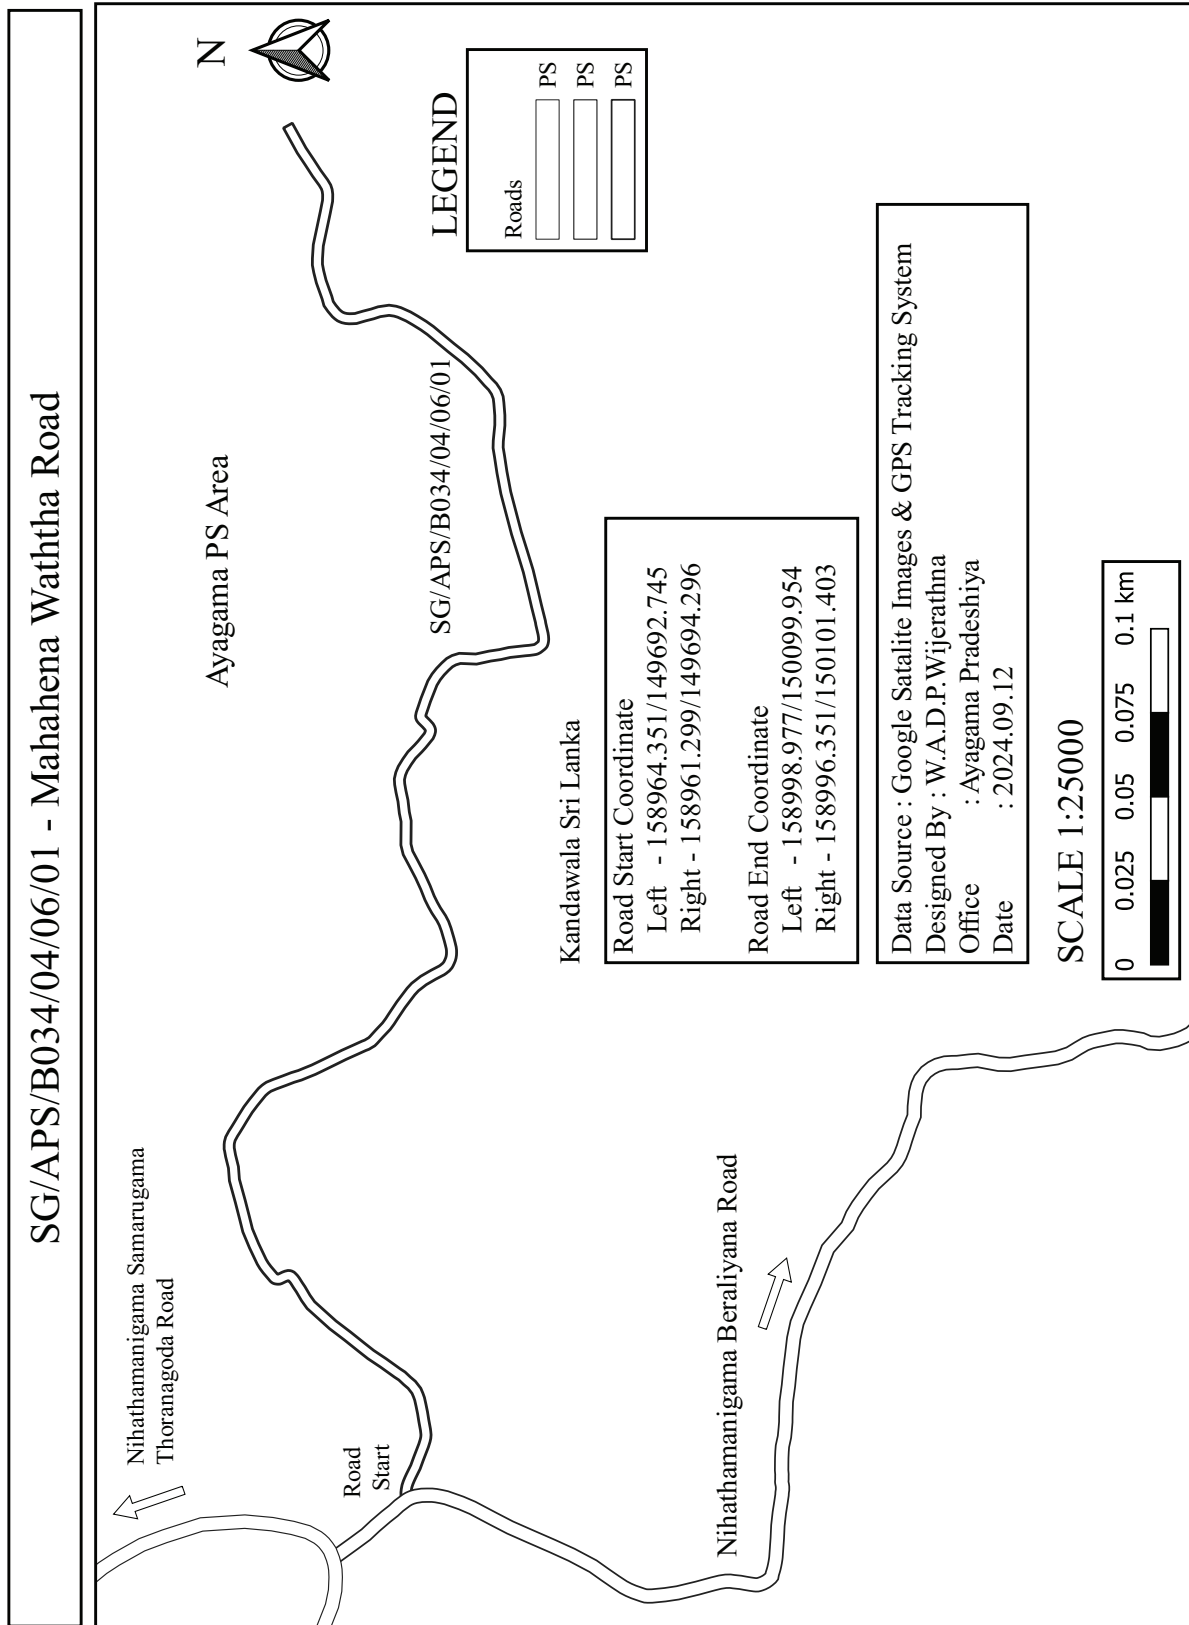

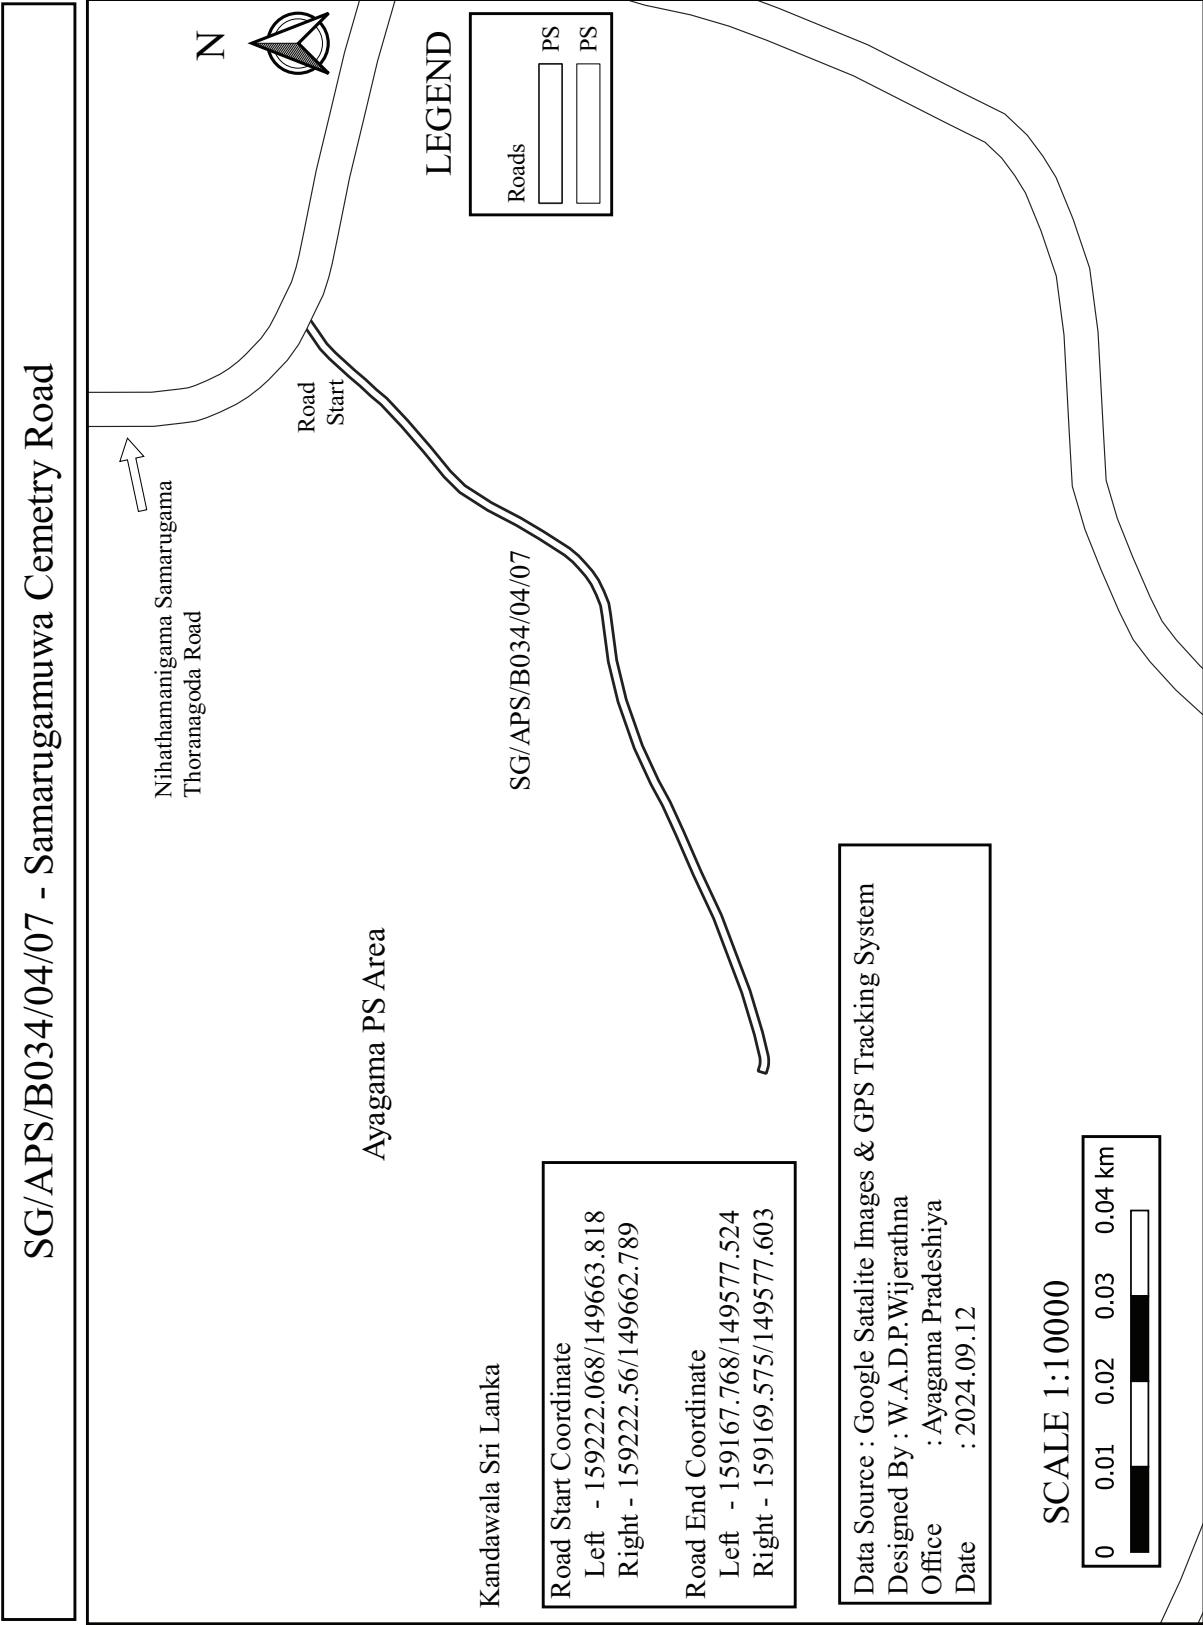


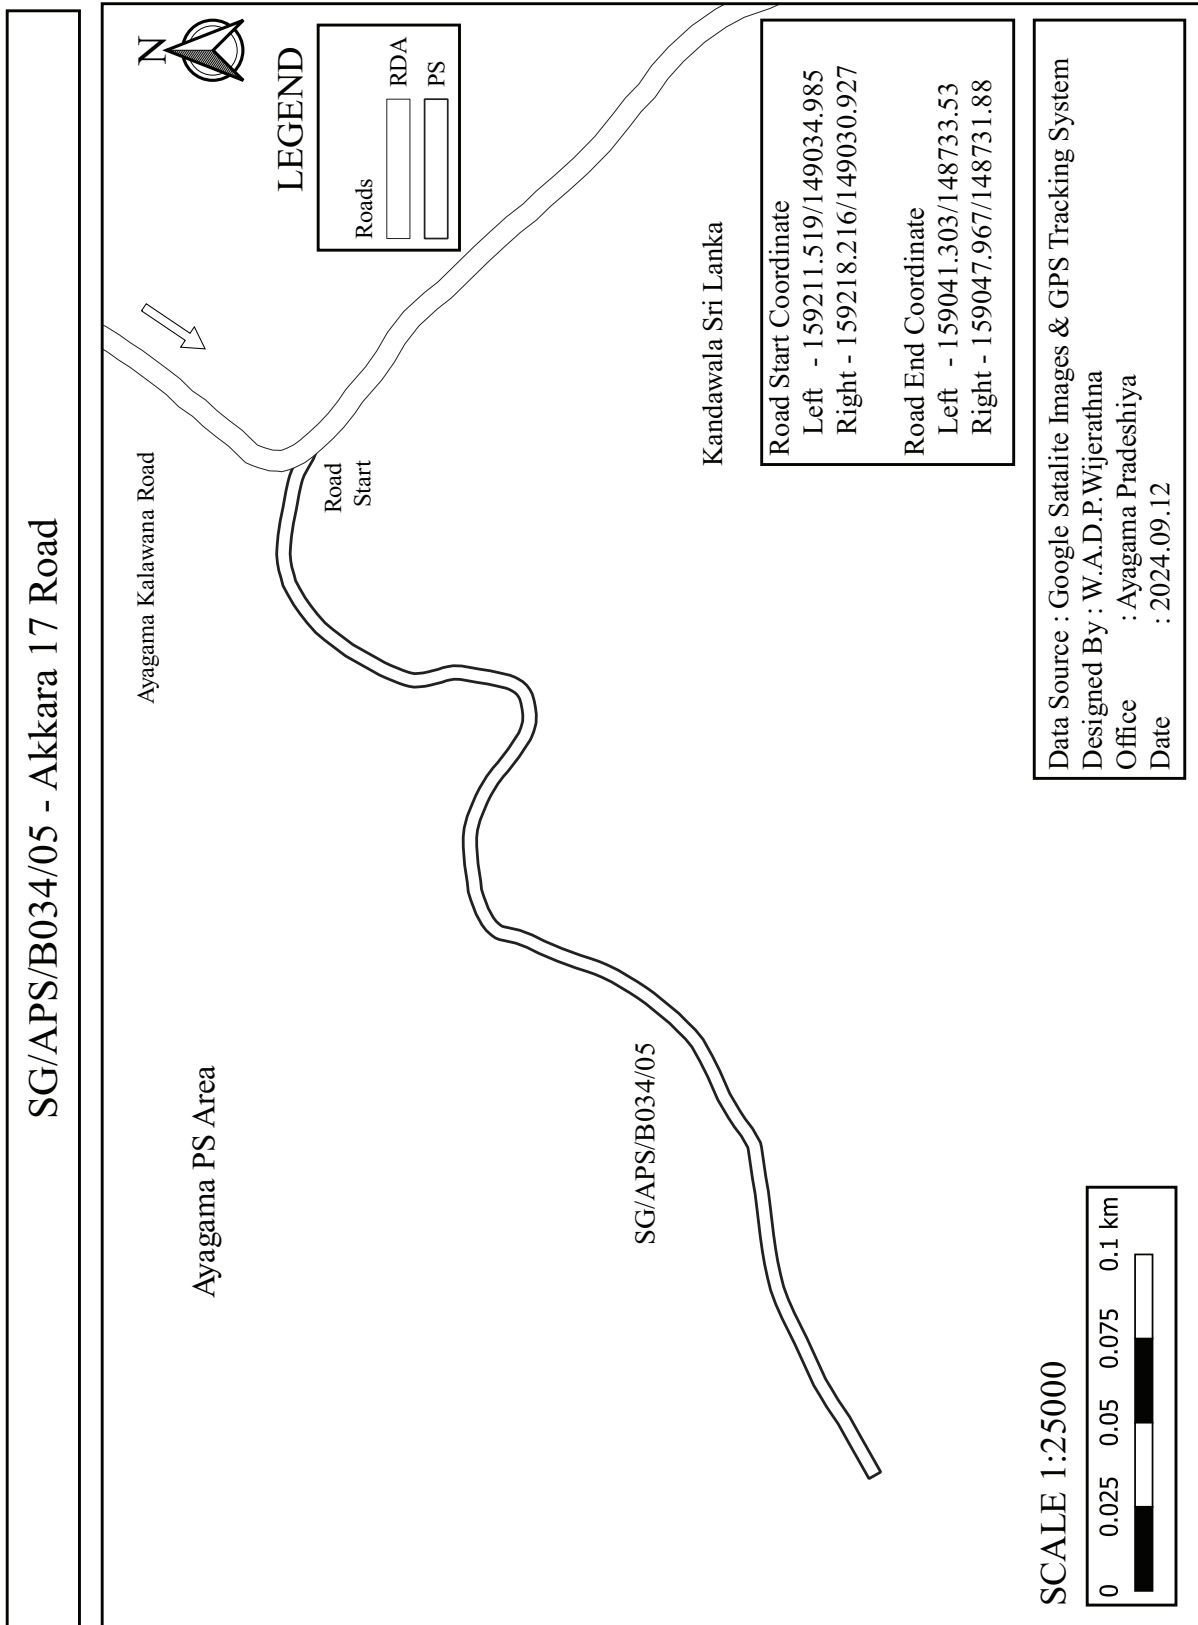


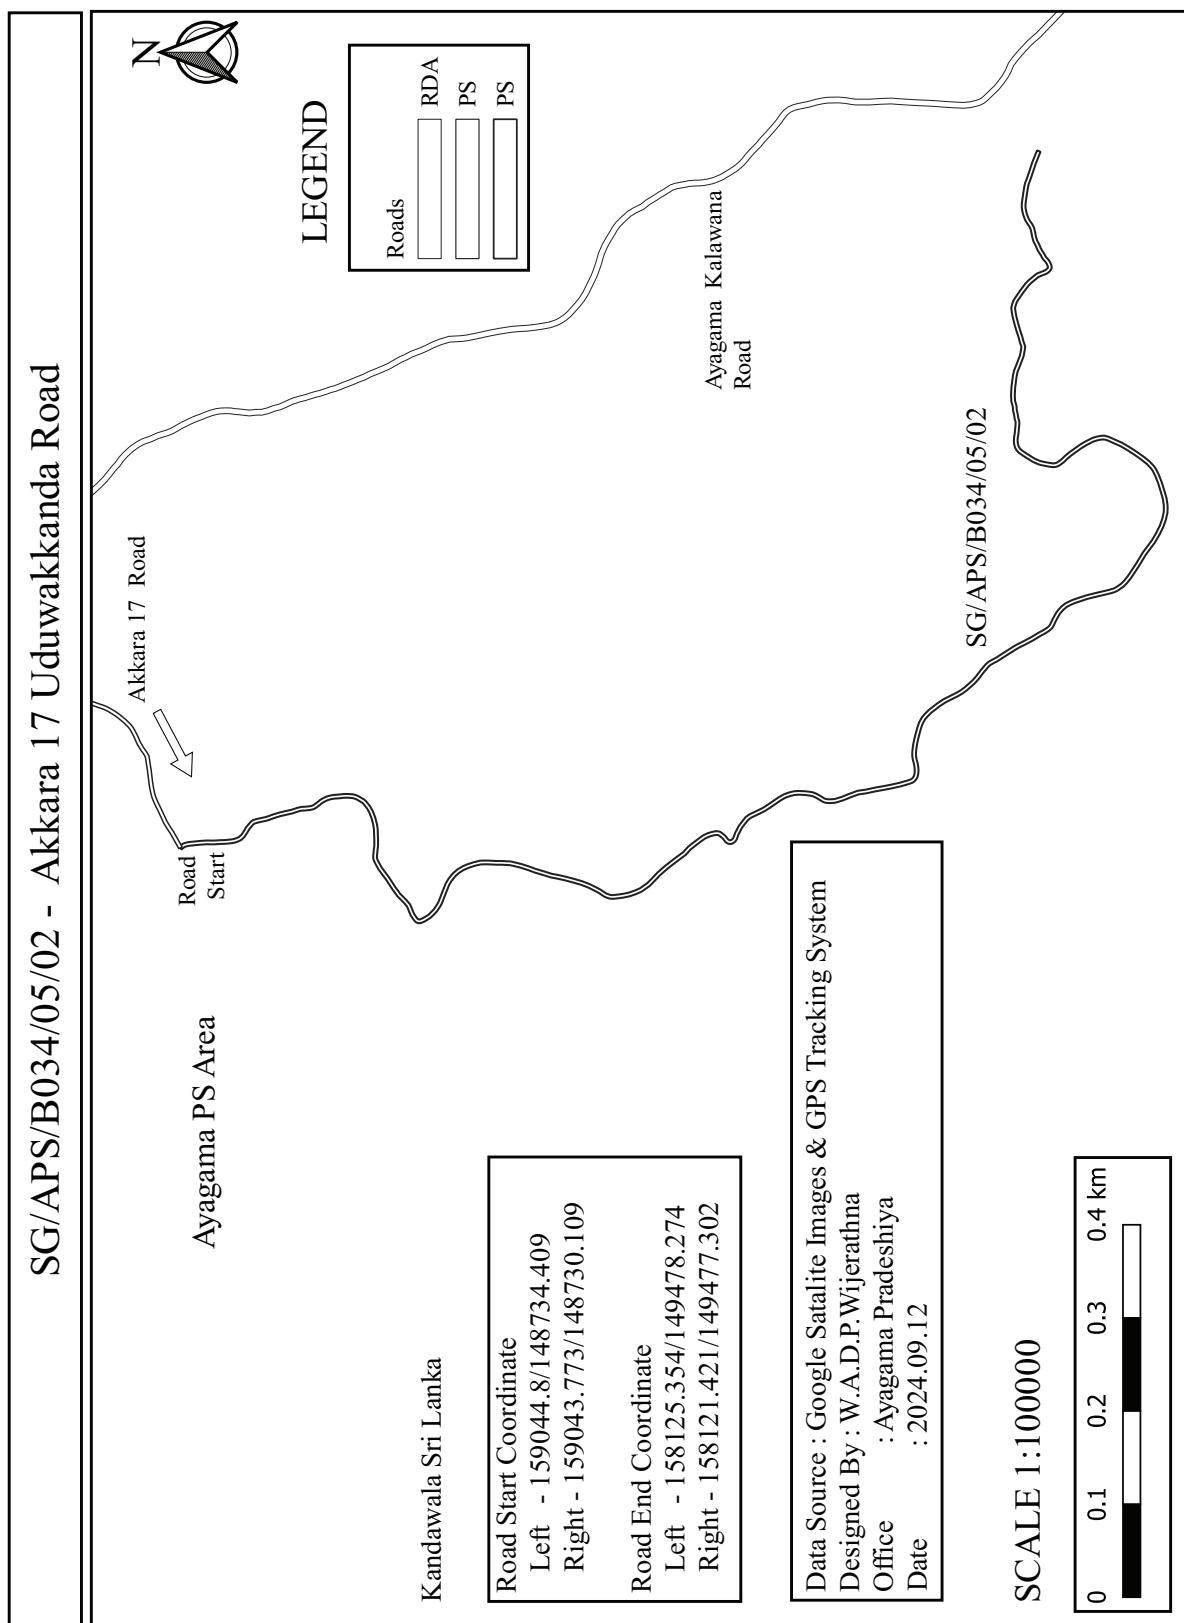

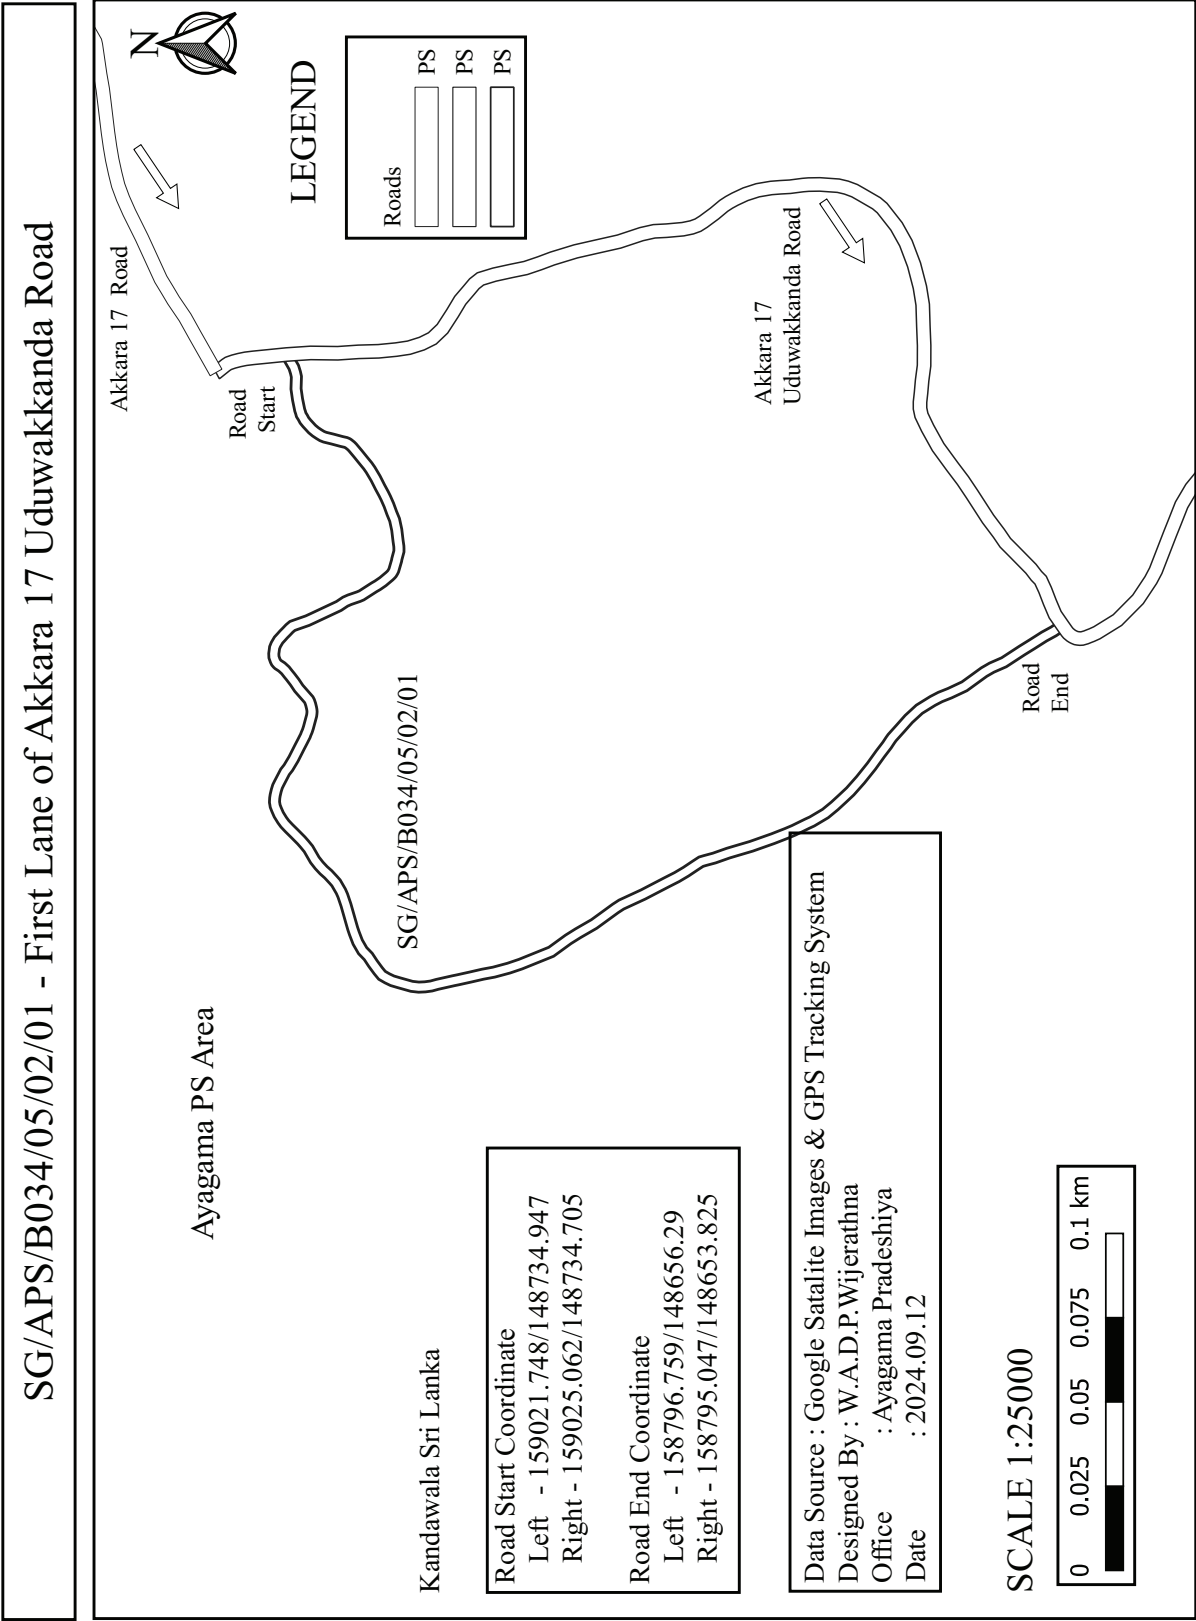



SG/APS/B034/05/02/01/01 - First By Pass of First Lane of Akkara 17 Uduwakkanda Road

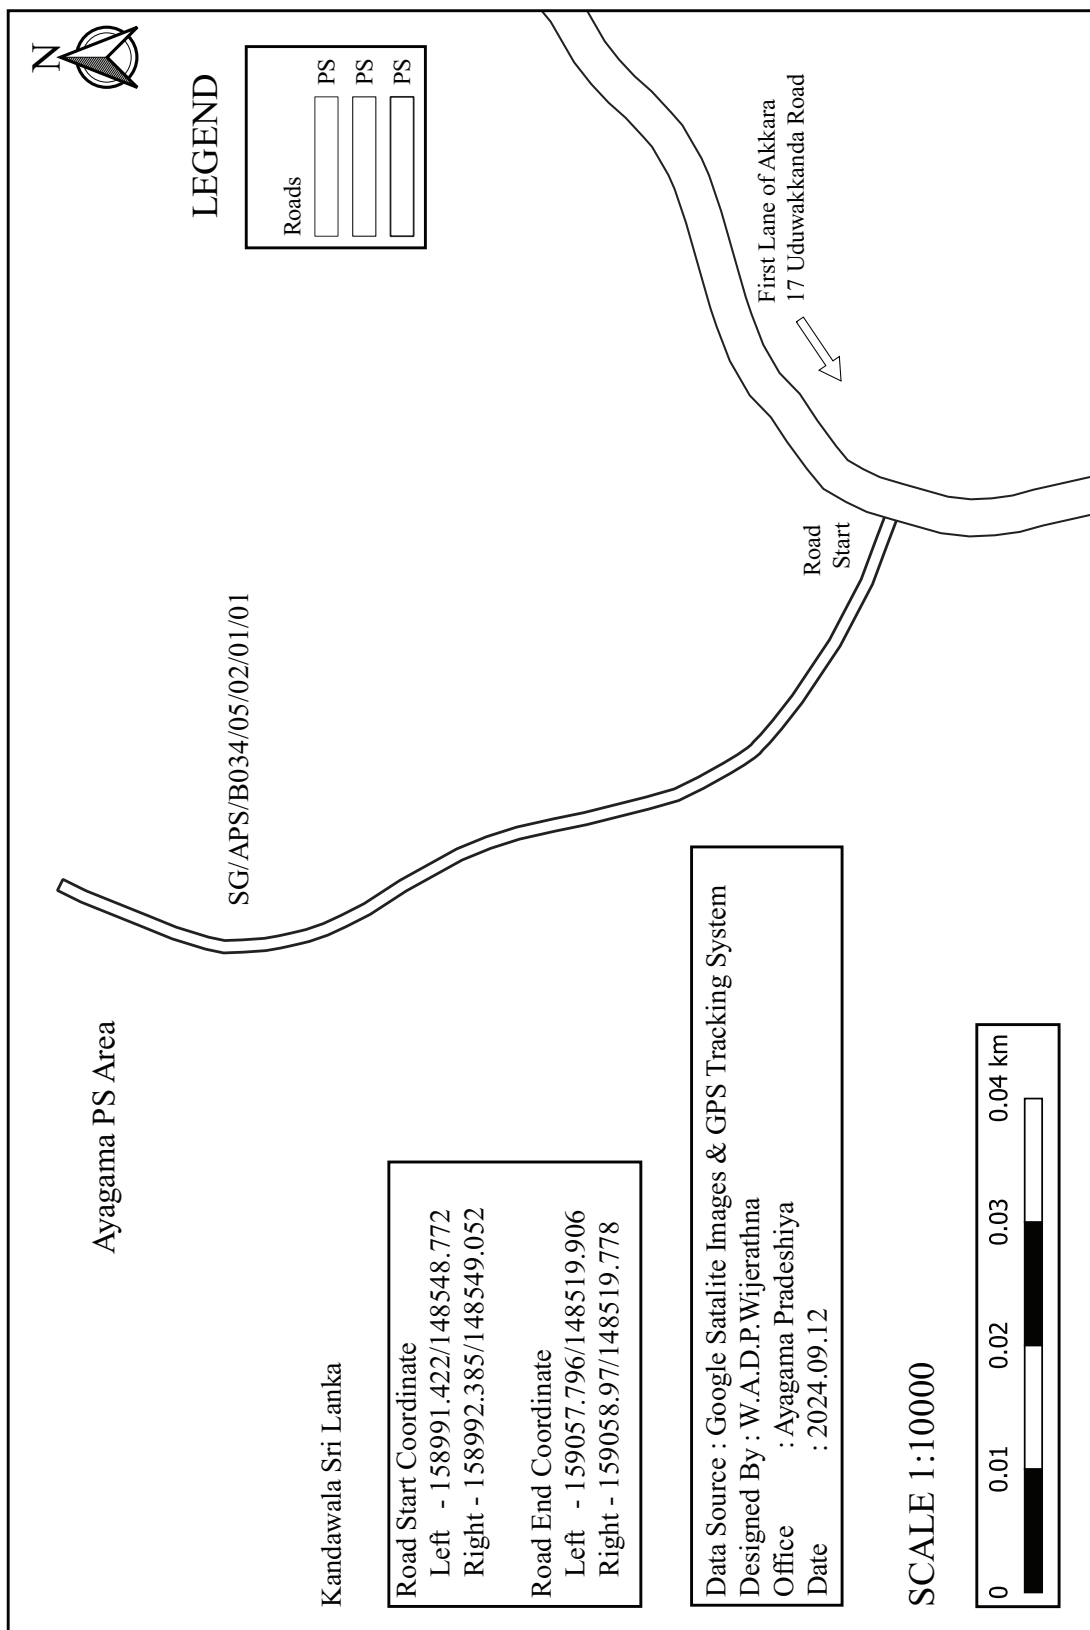

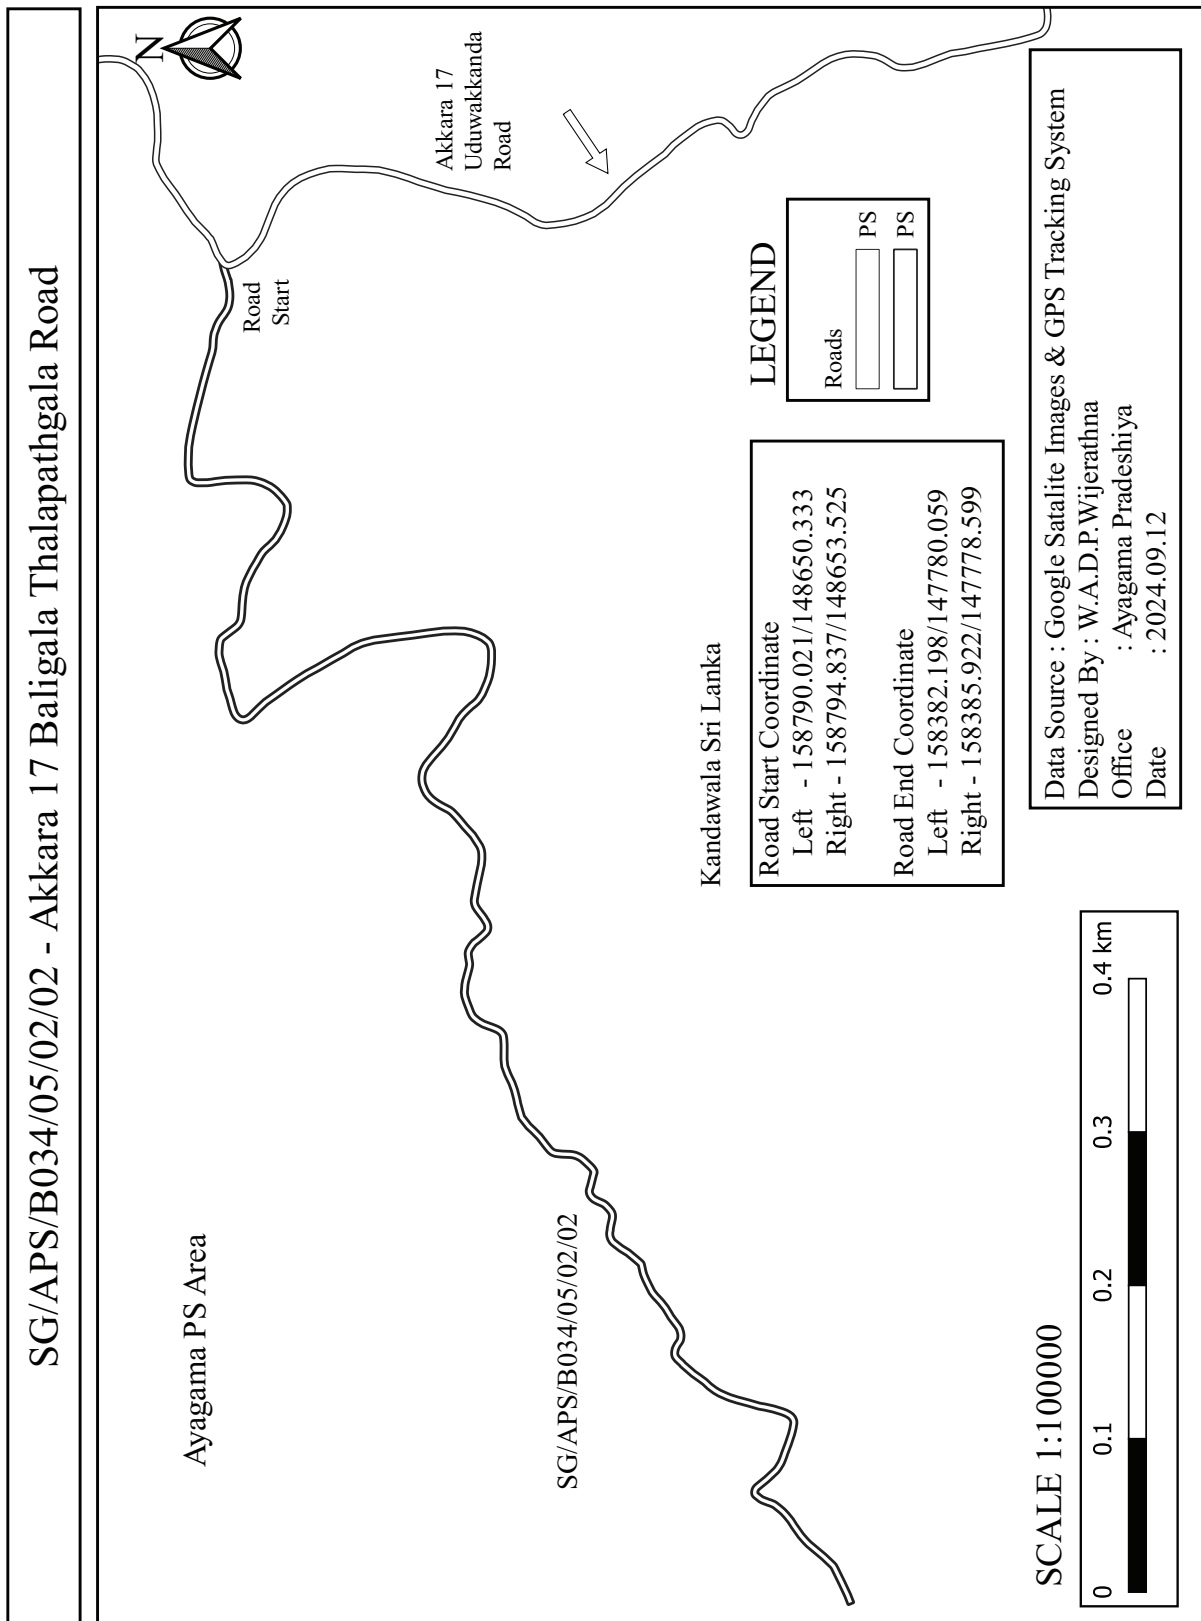



SG/APS/B034/05/02/02/01 - First Lane of Akkara 17 Baligala Thalapathgala Road

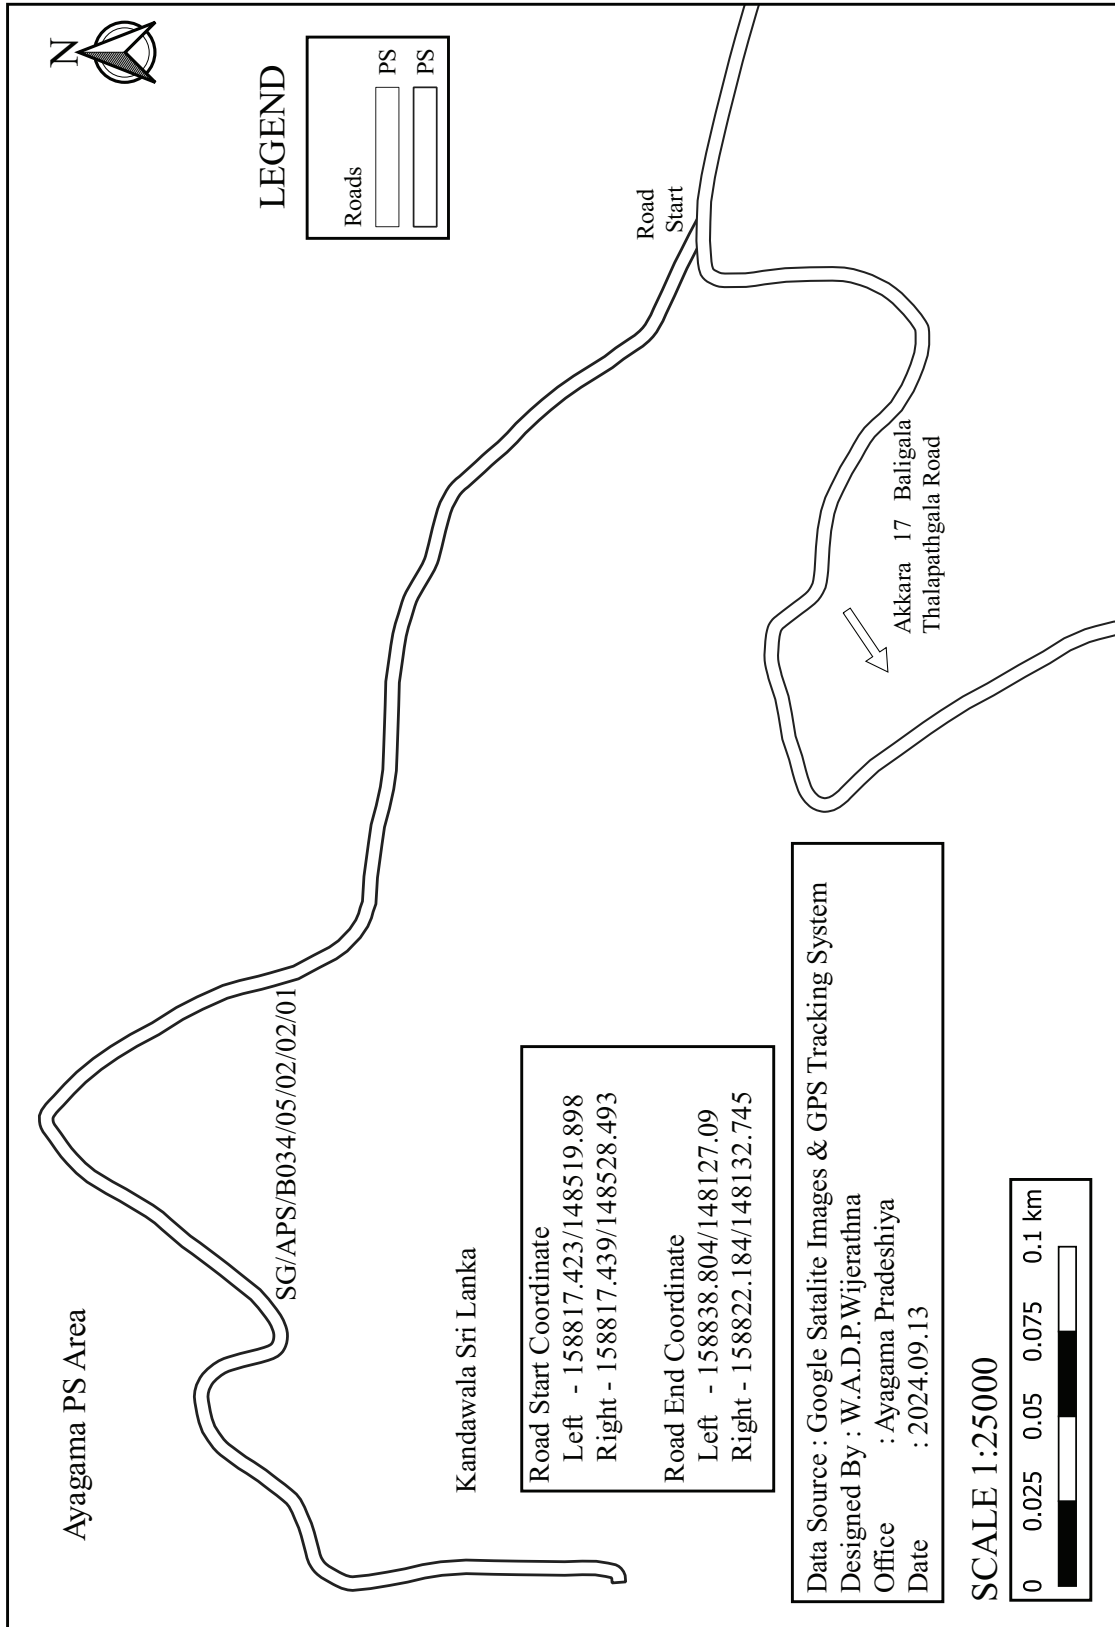


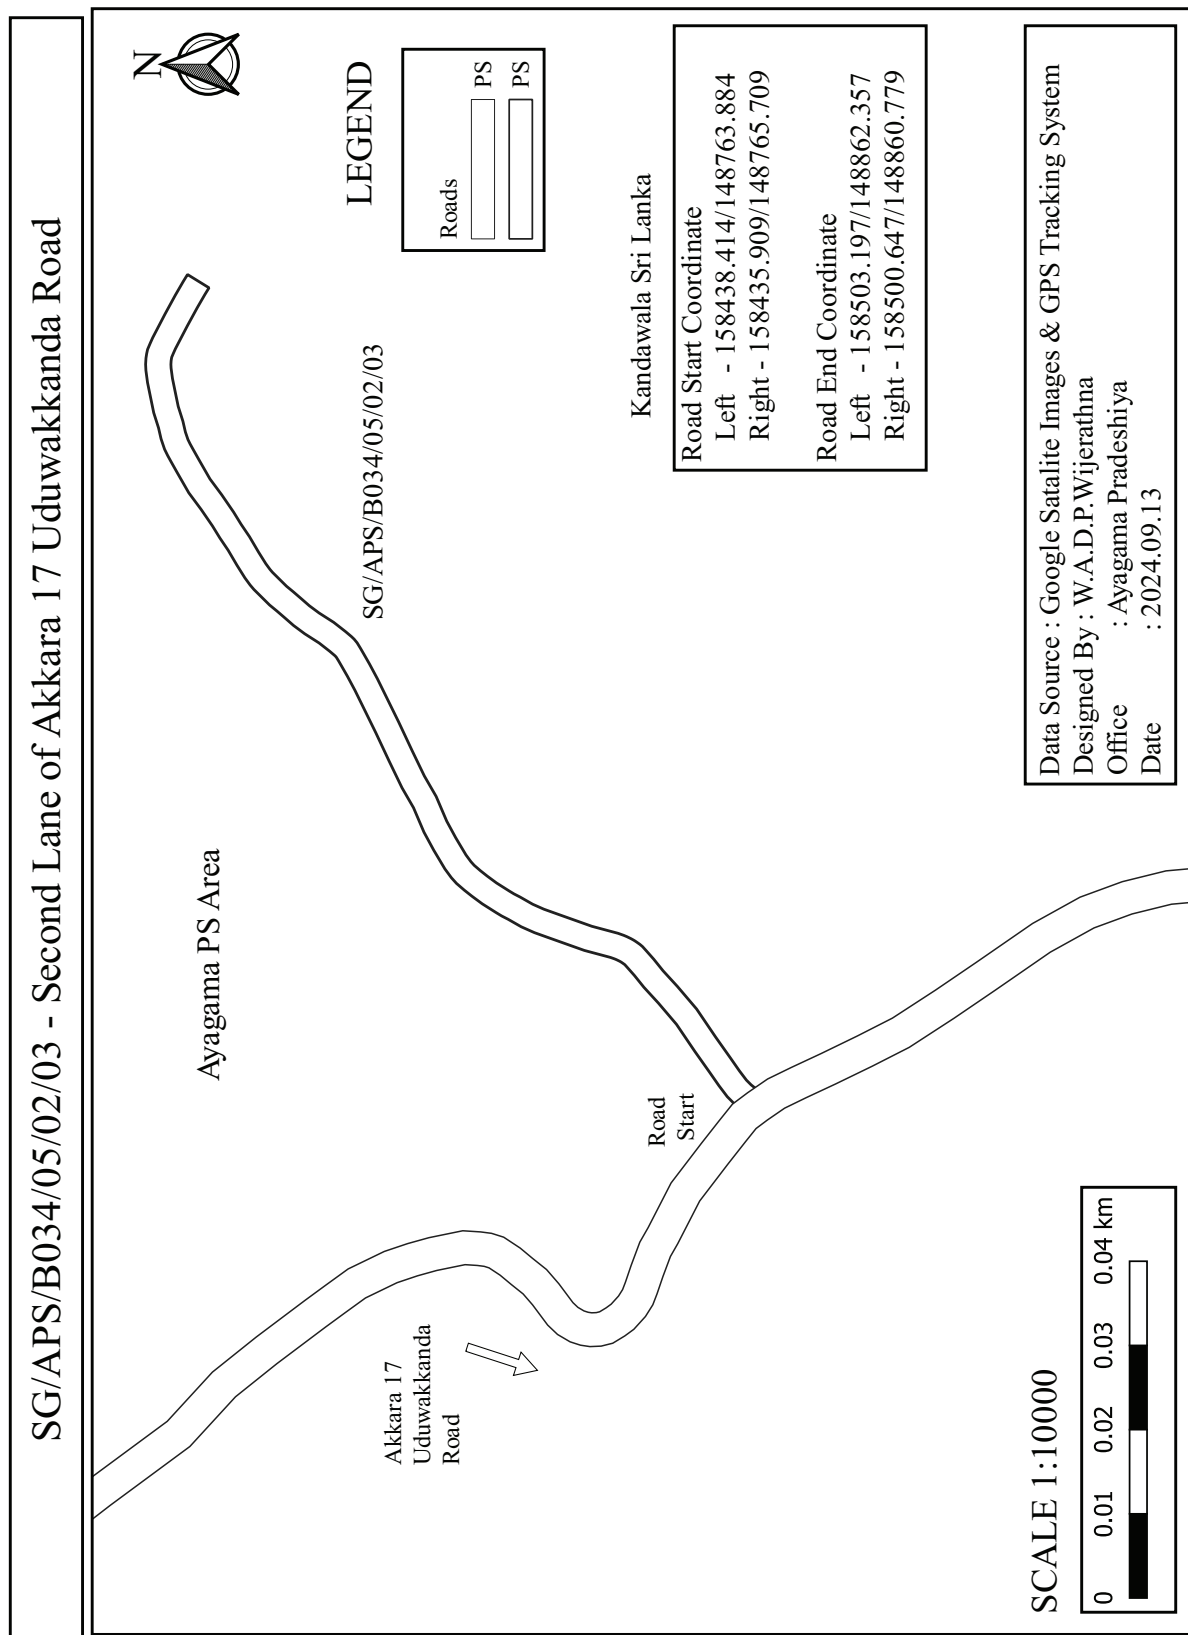



SG/APS/B034/06 -Ereporuwa First Lane

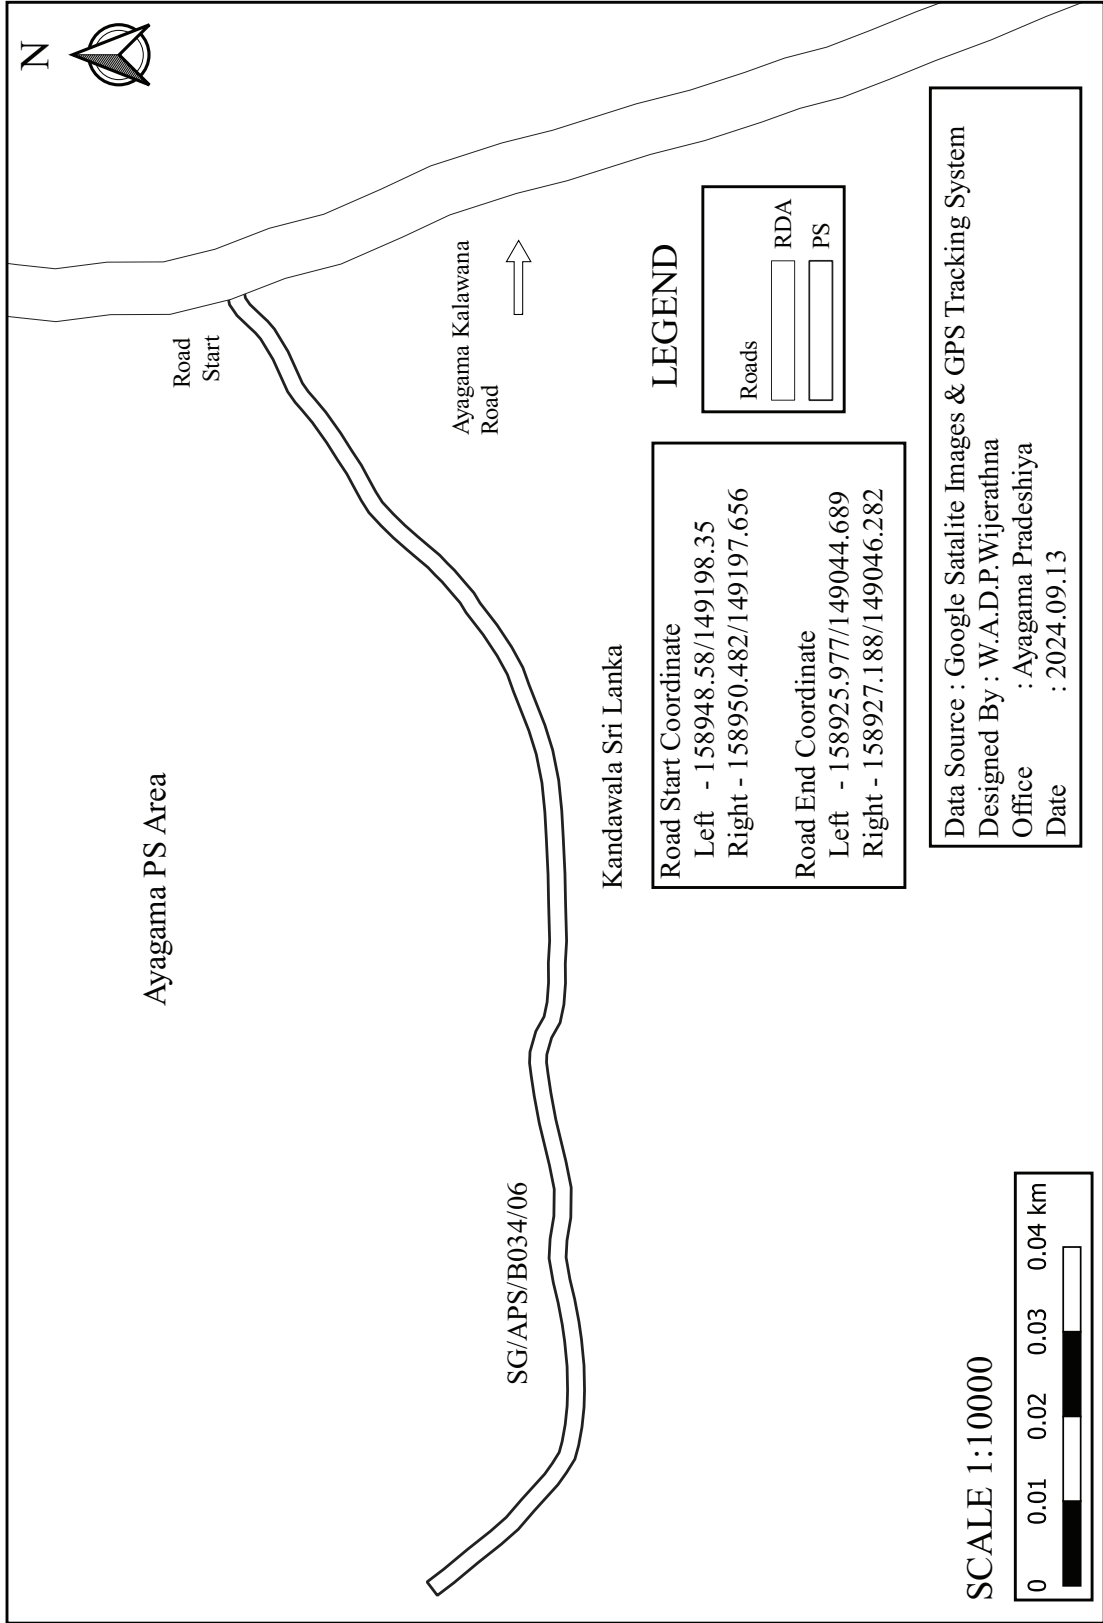


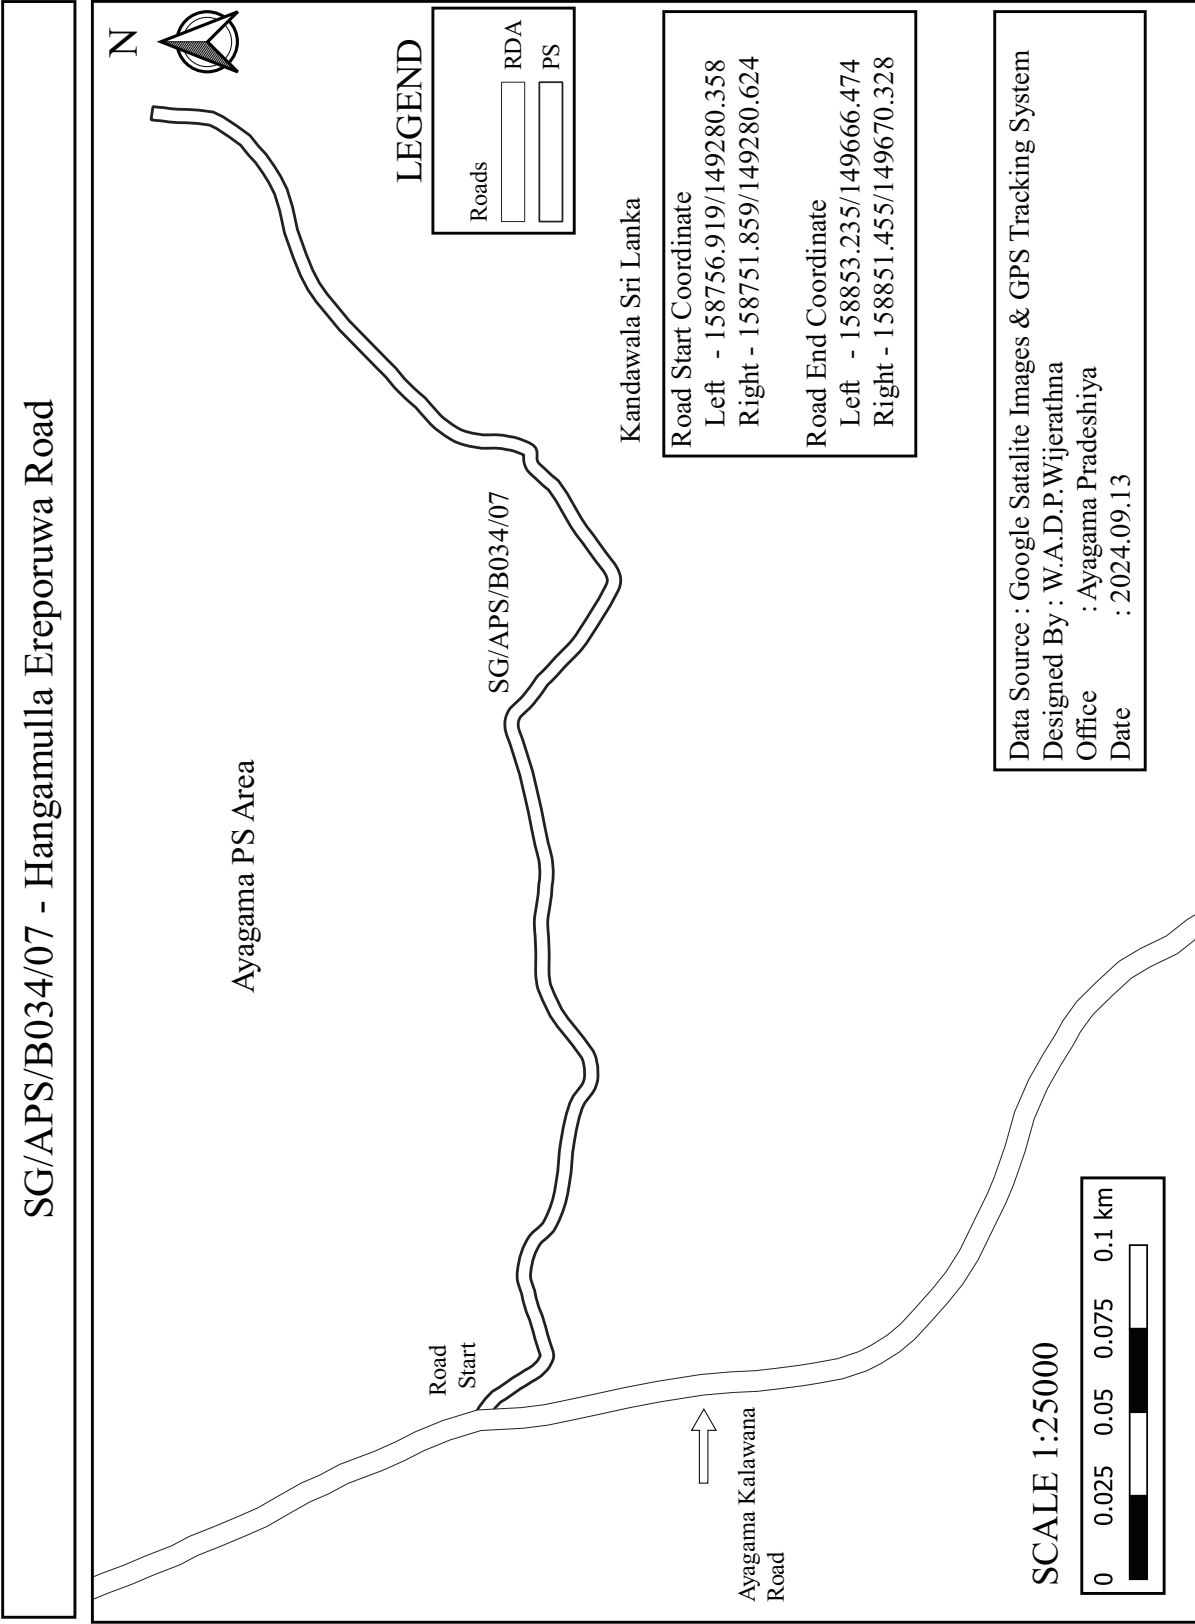


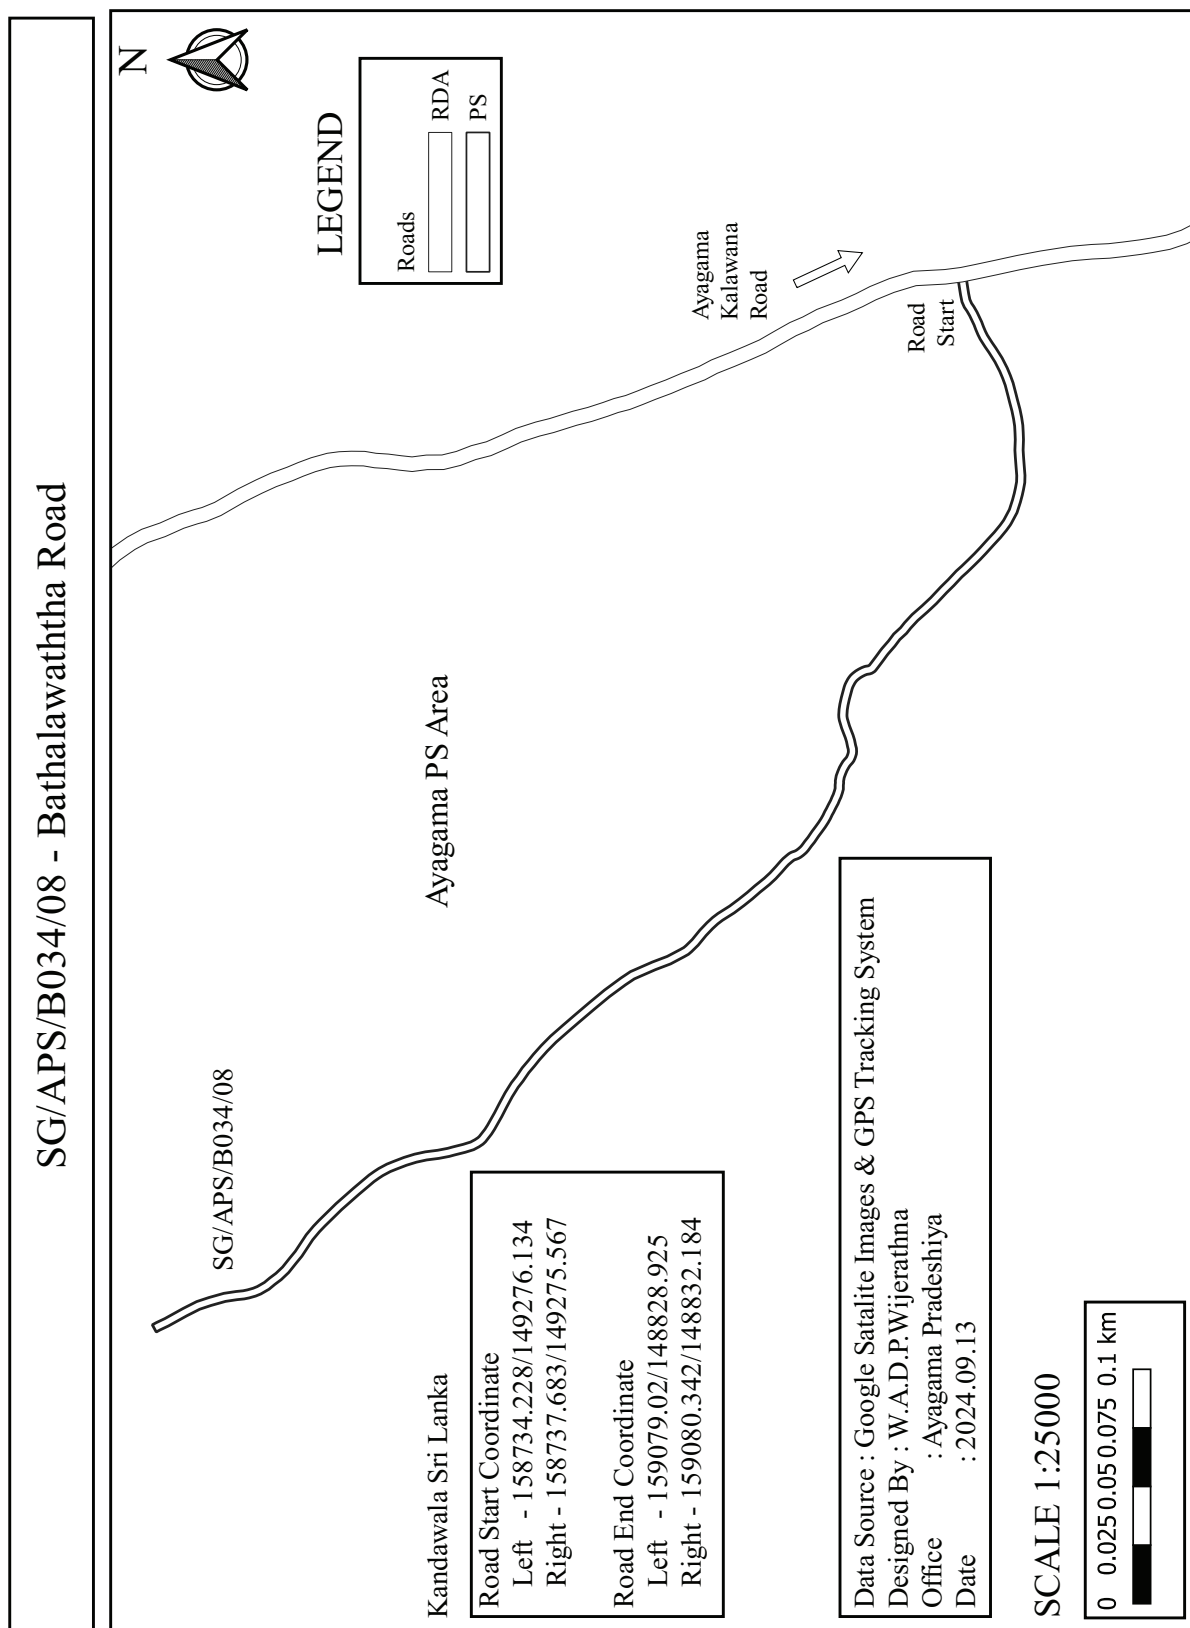


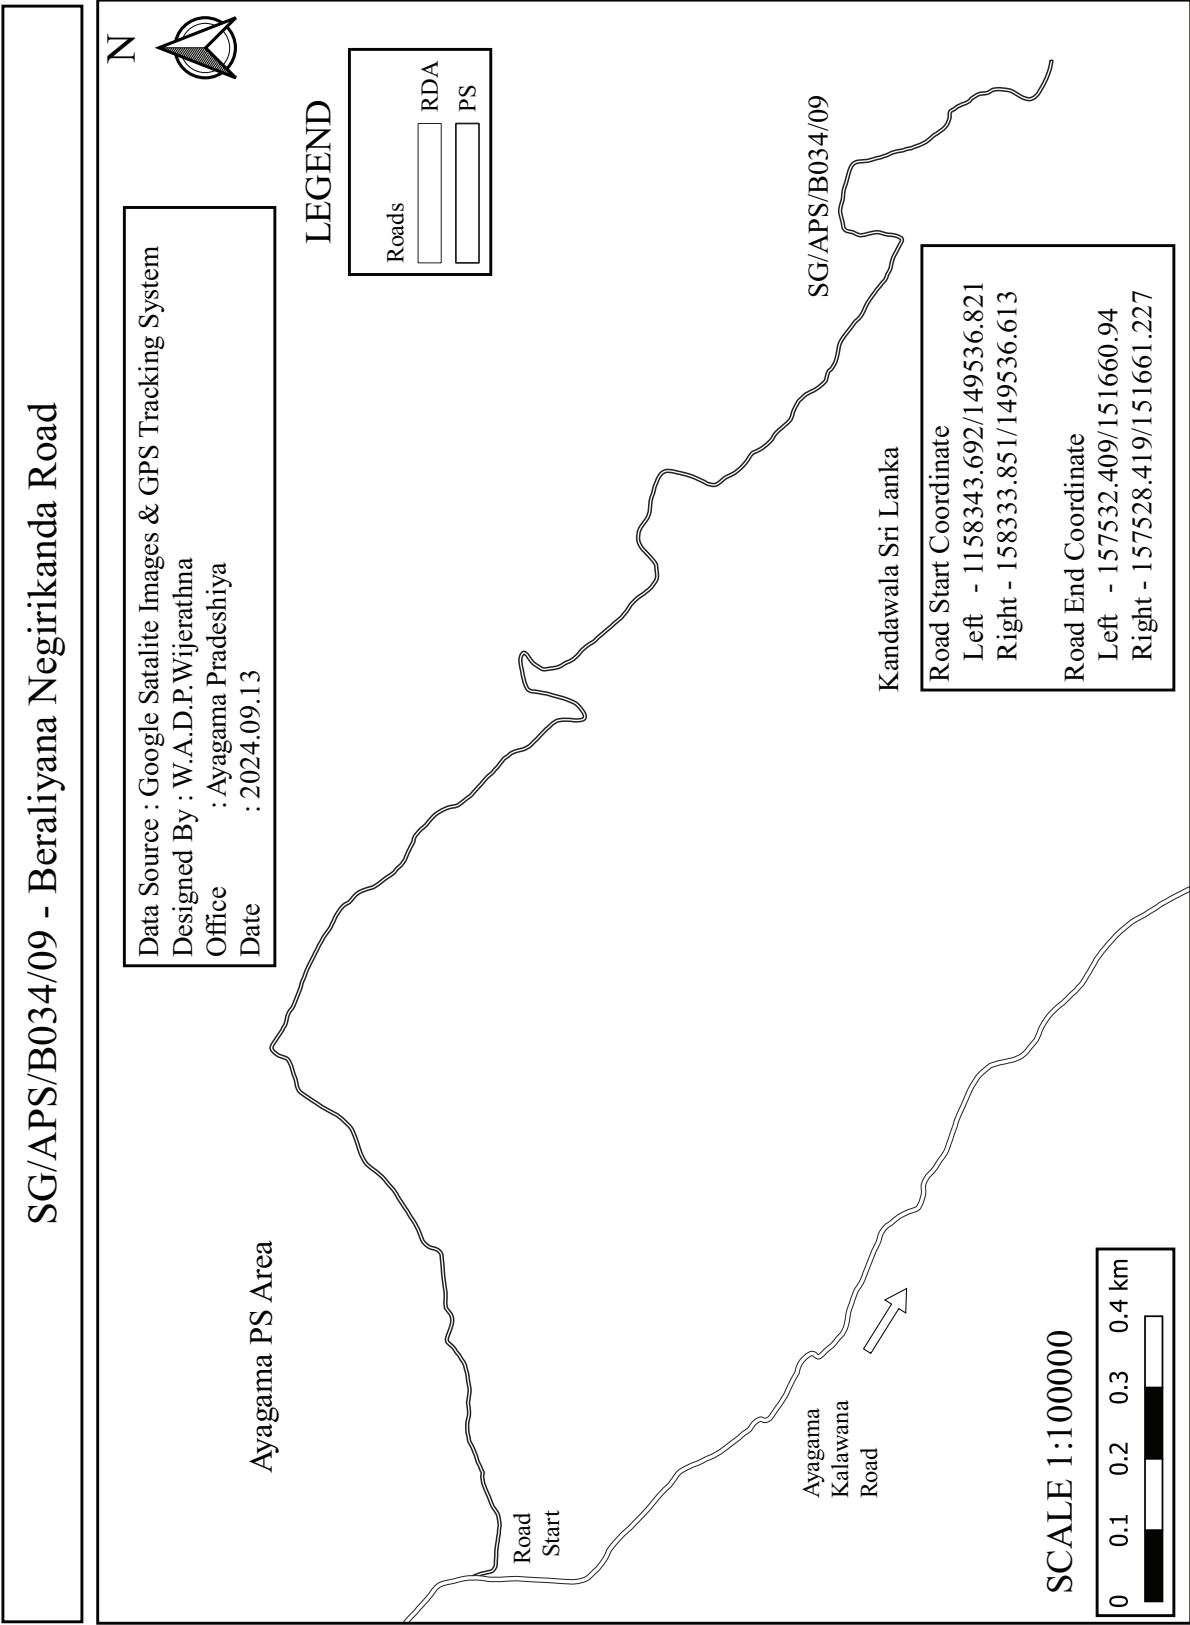


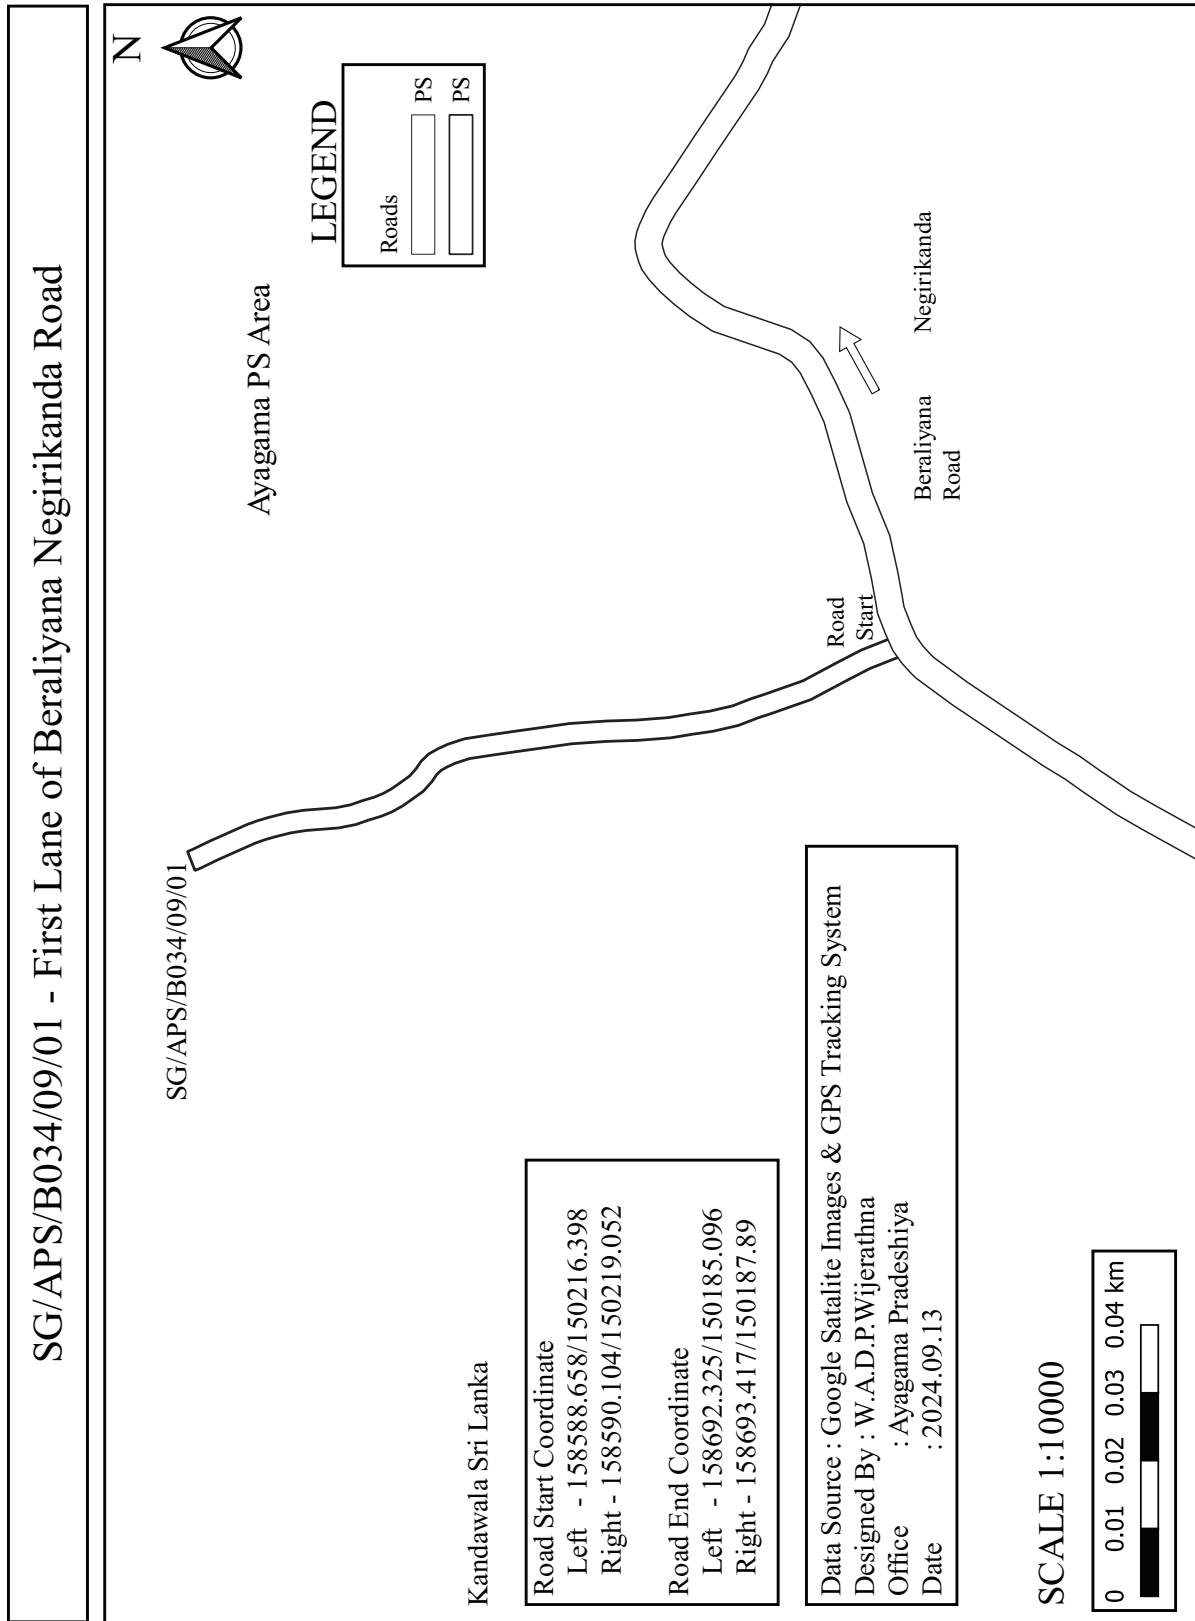


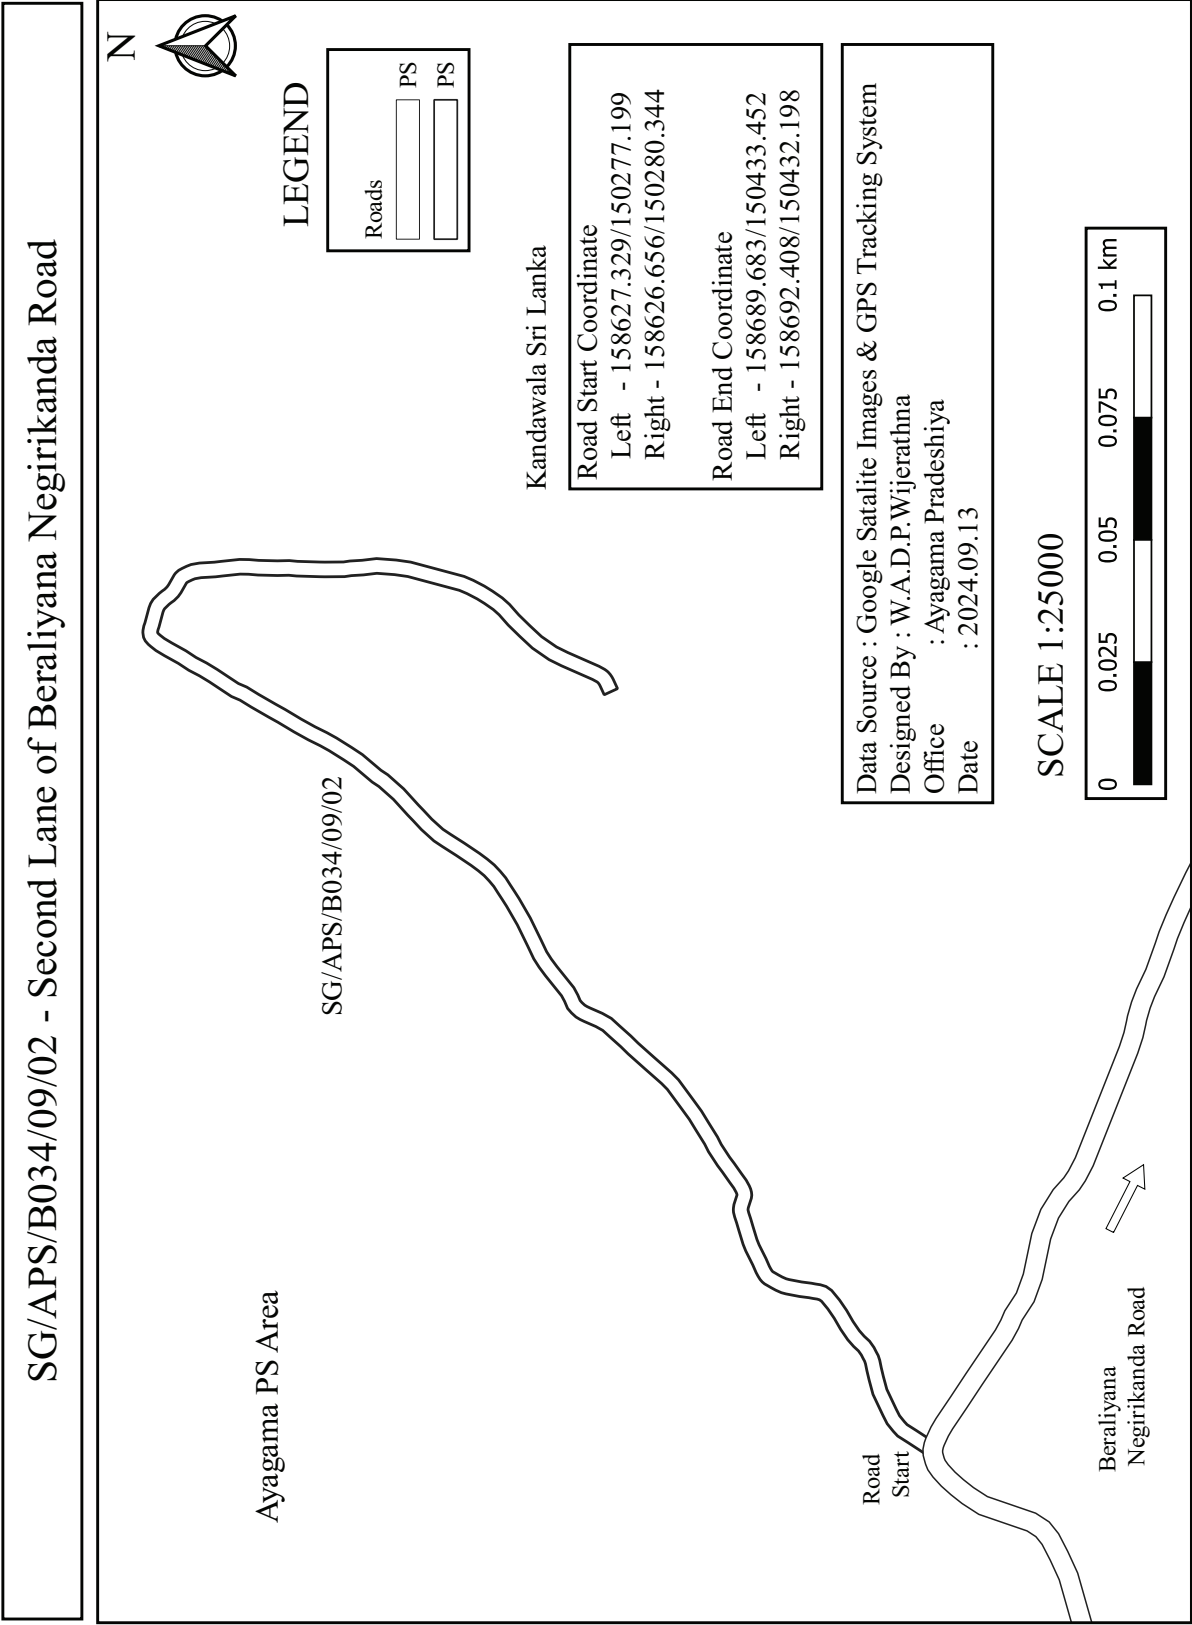


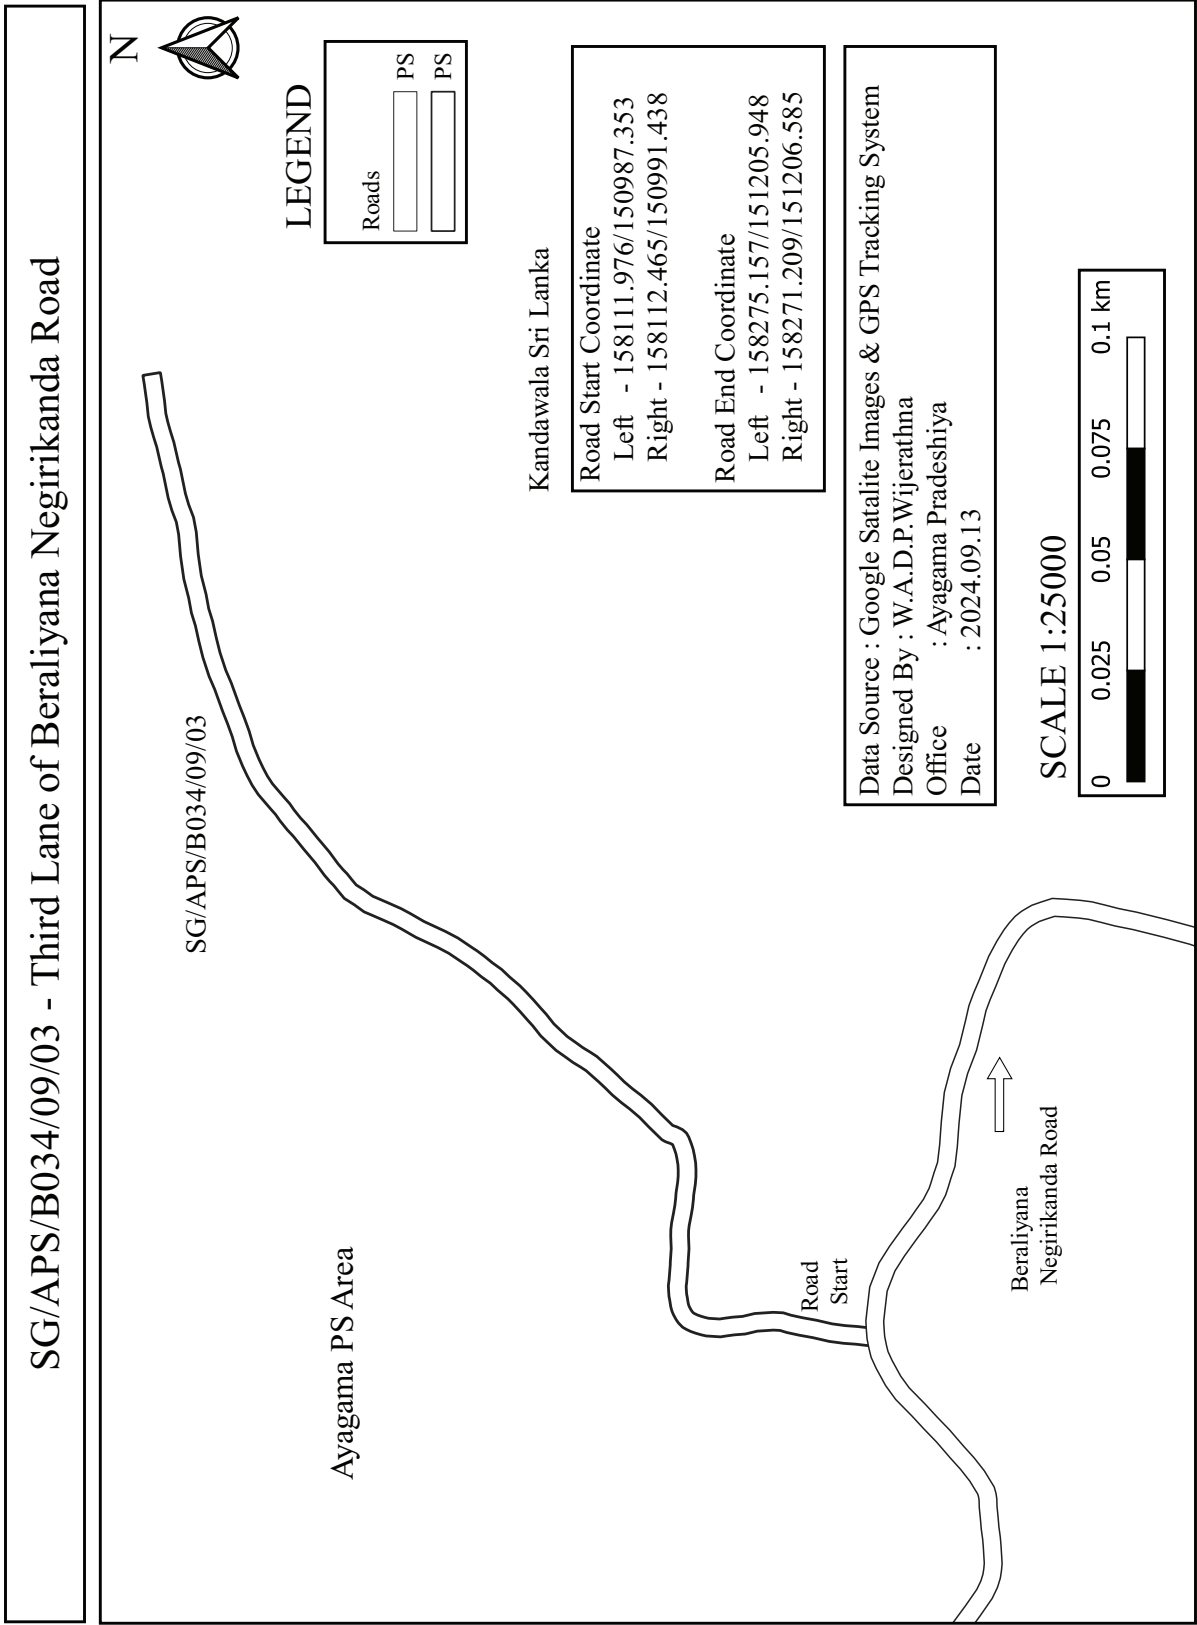


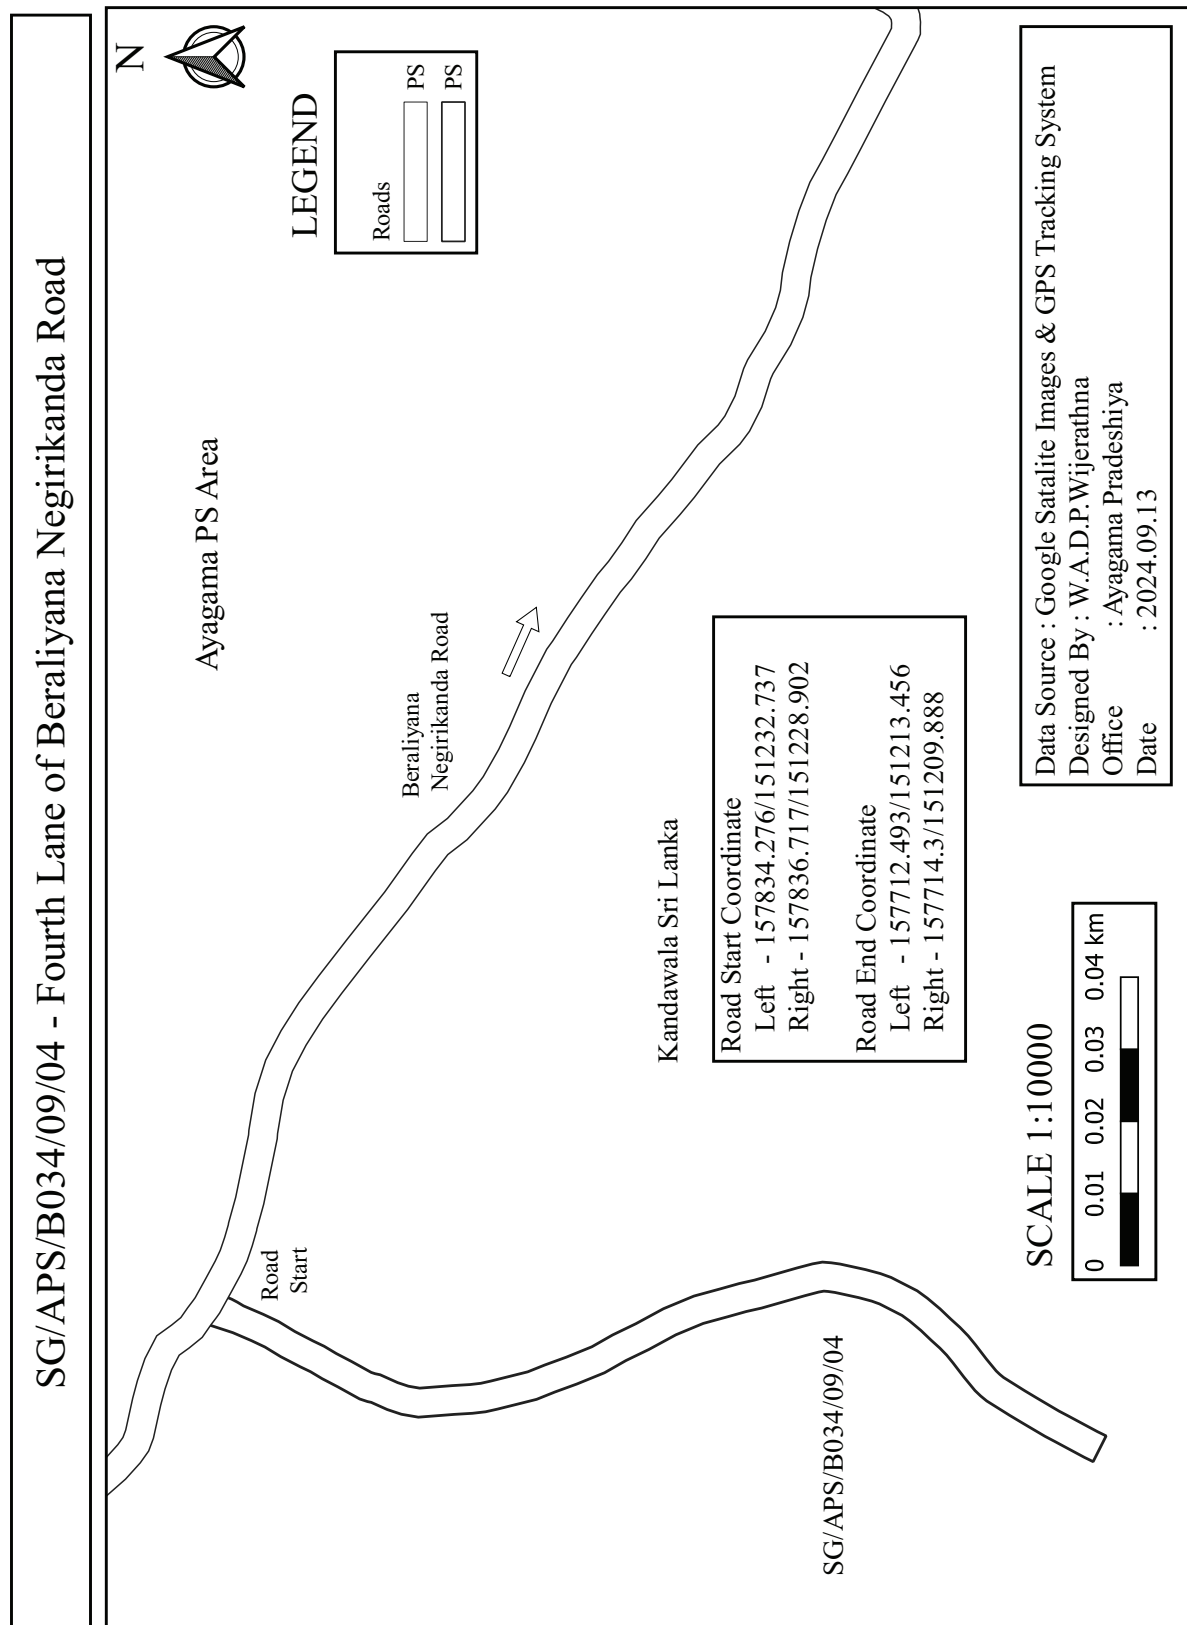


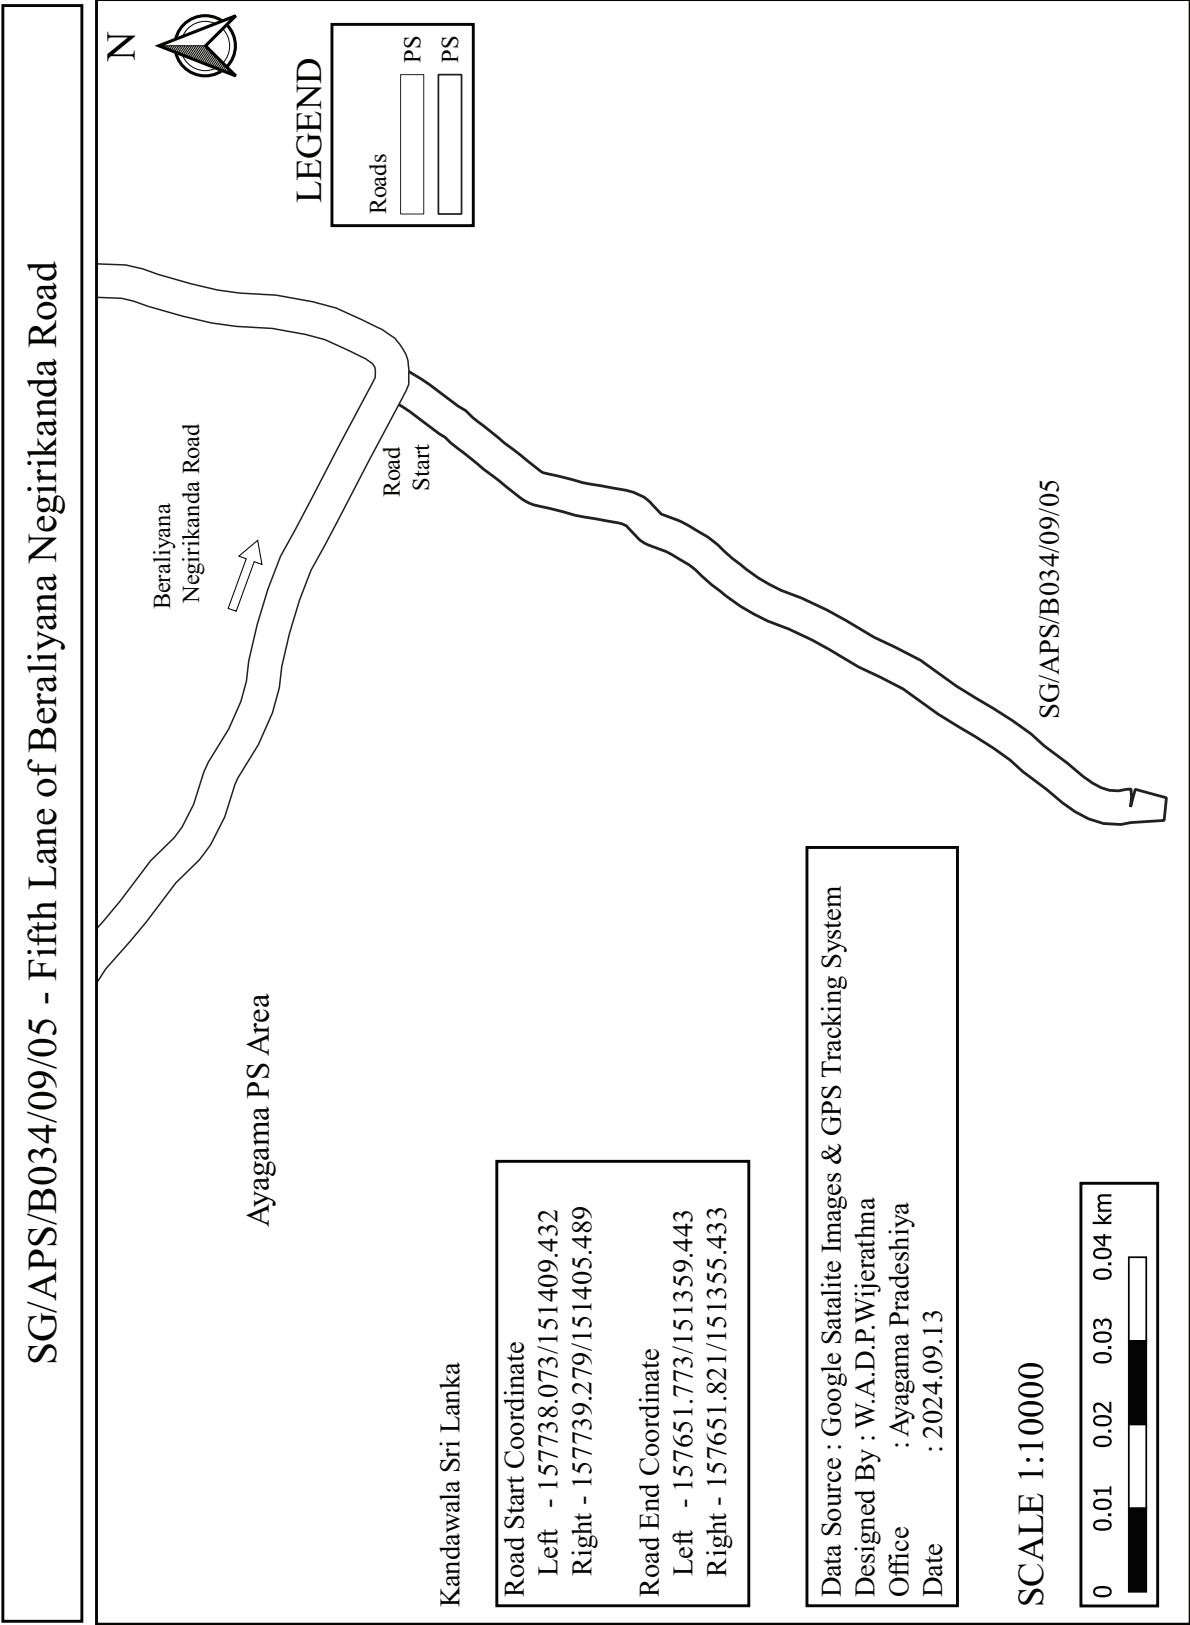


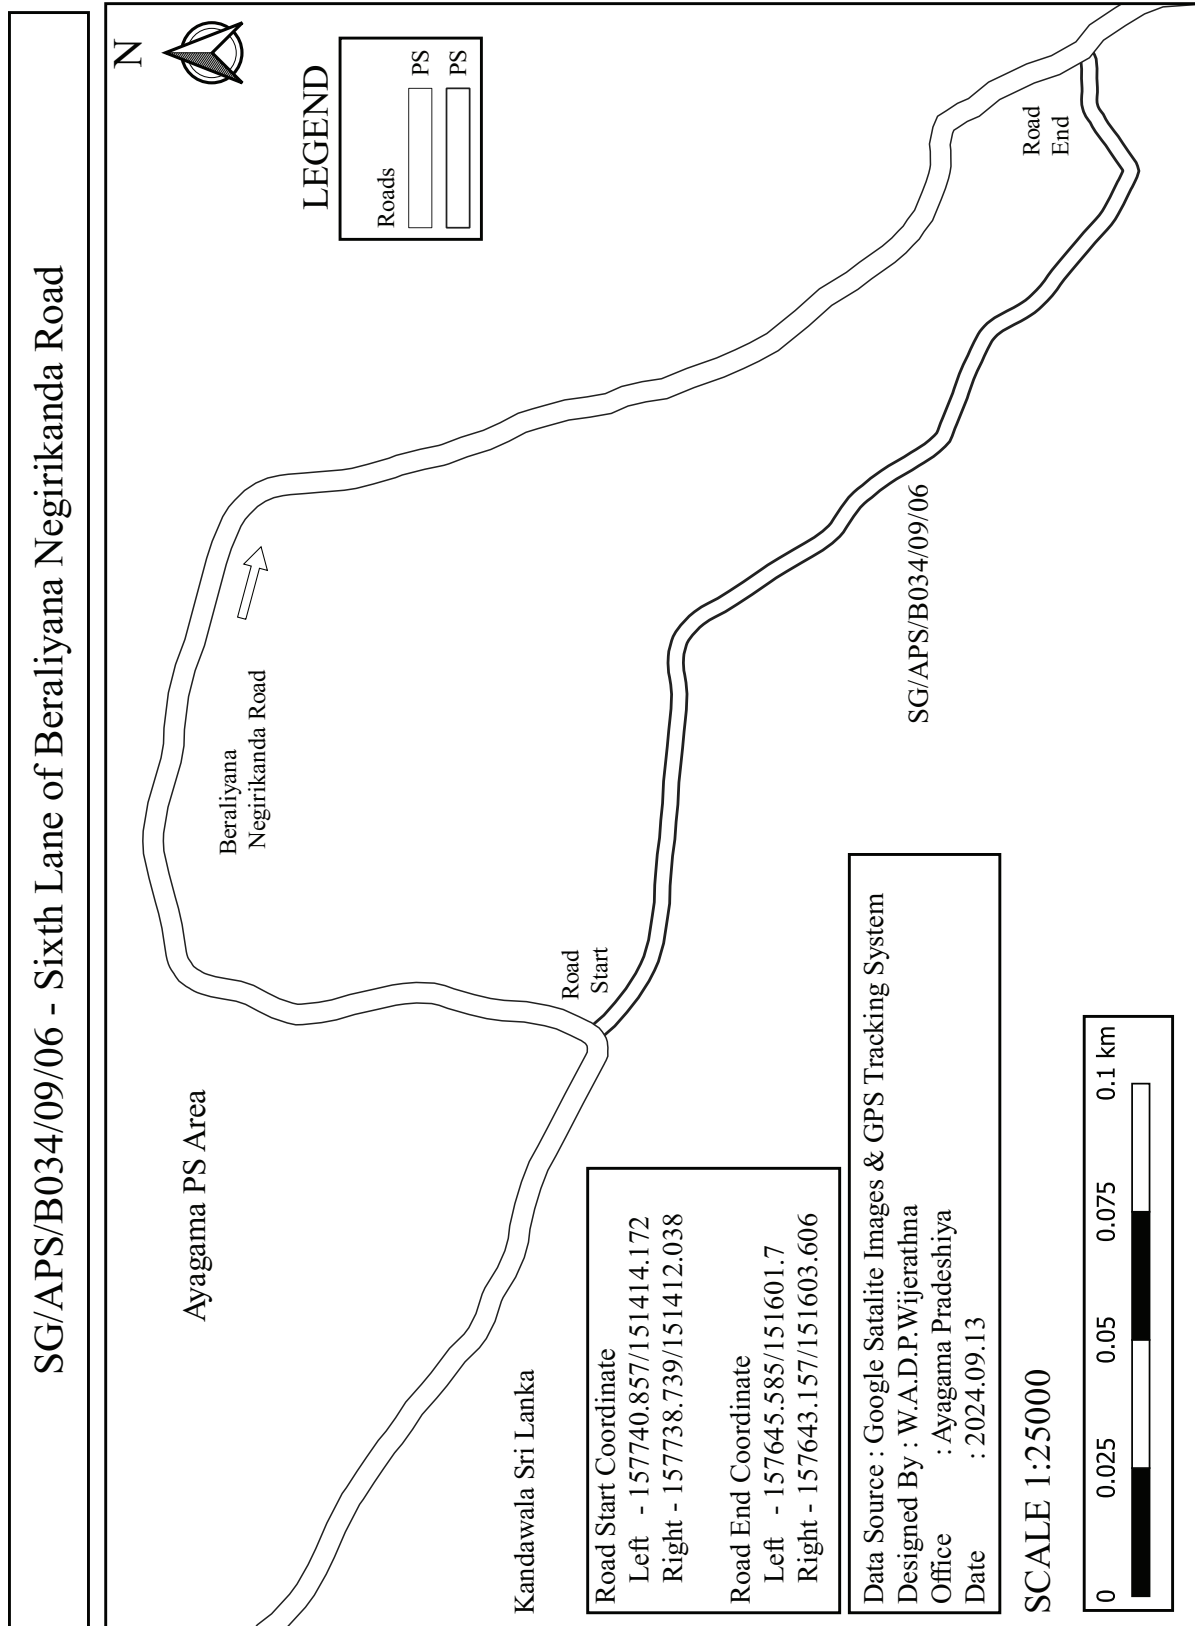


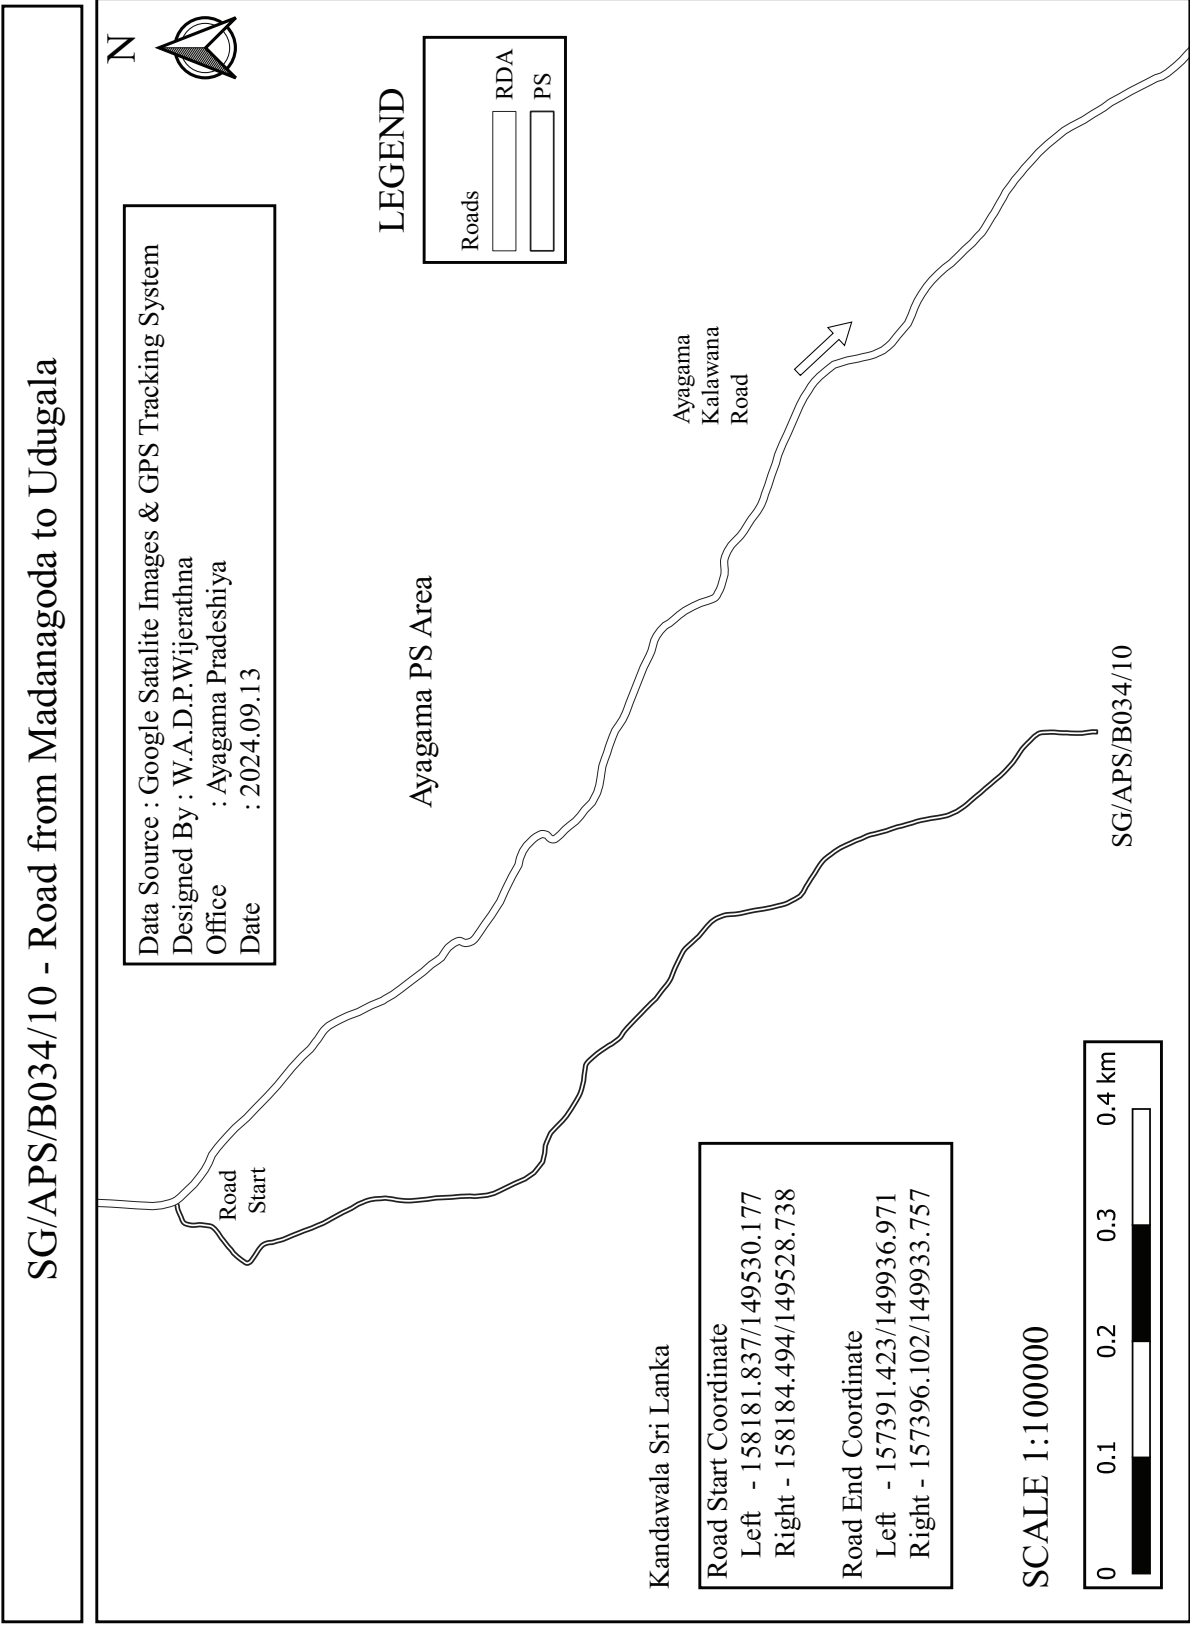


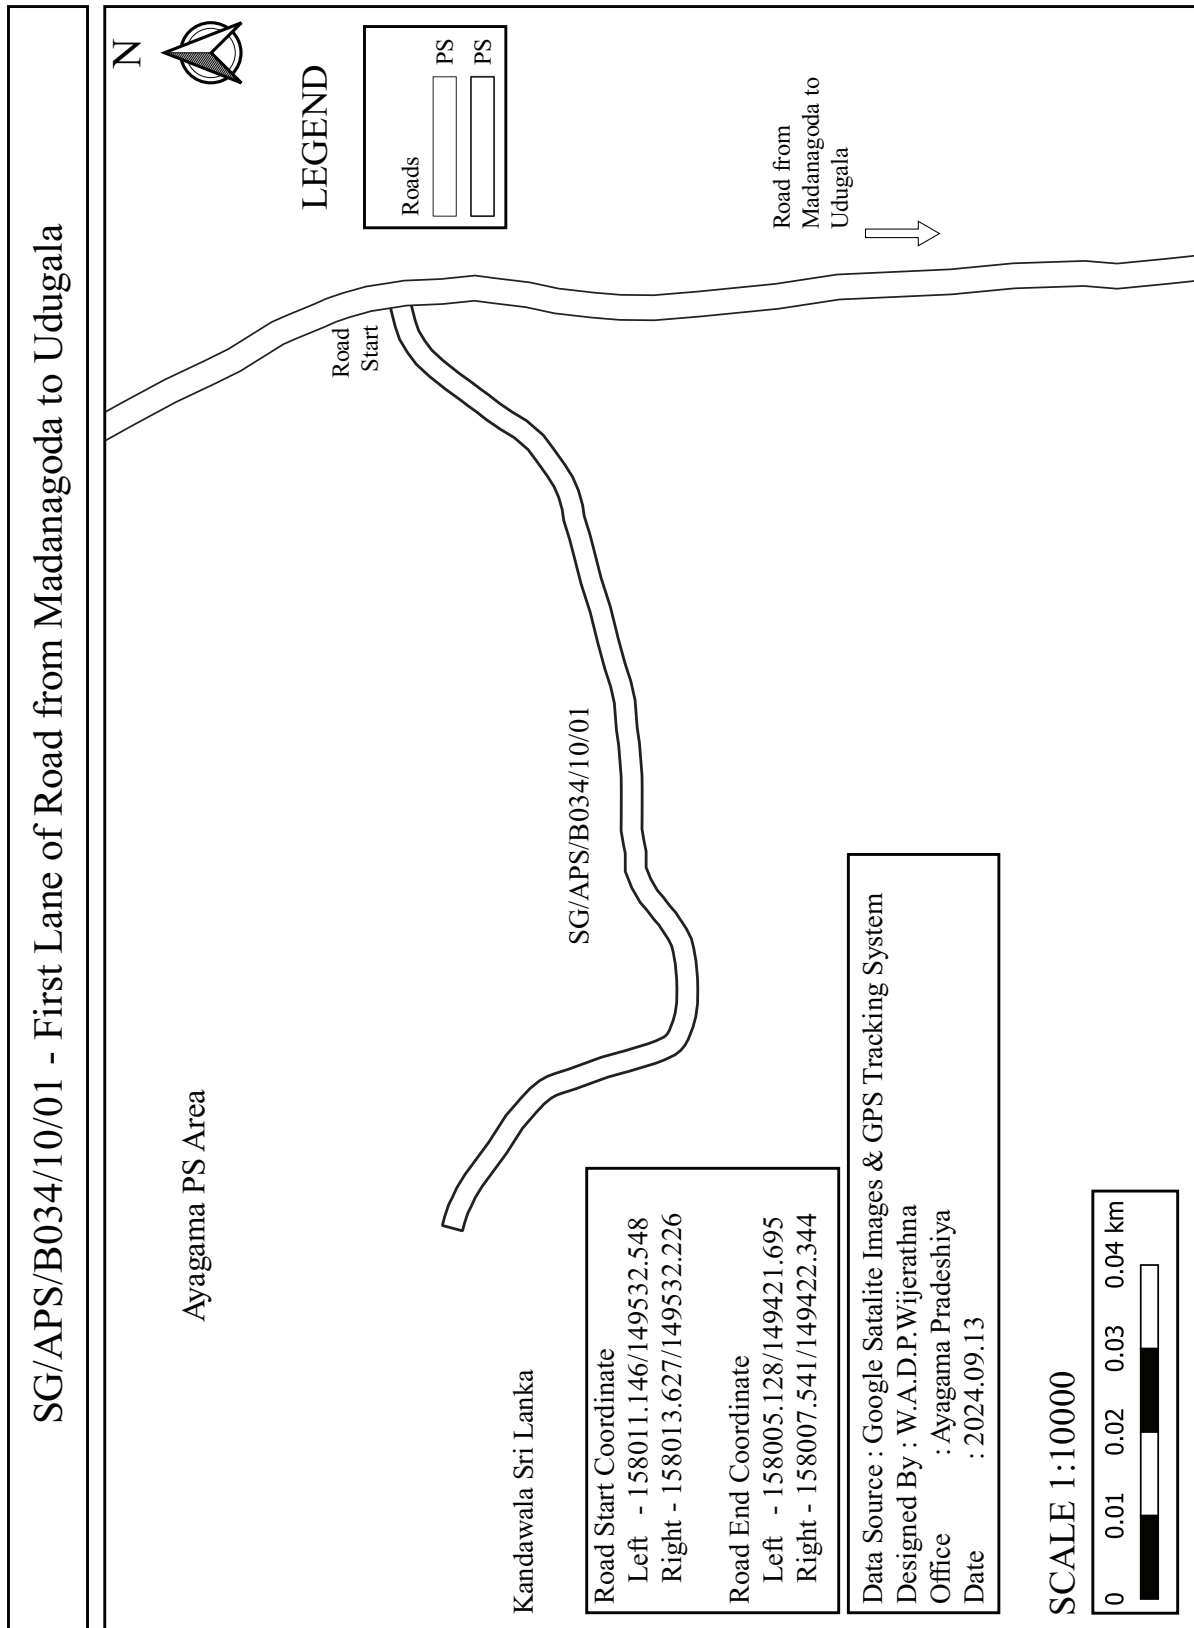


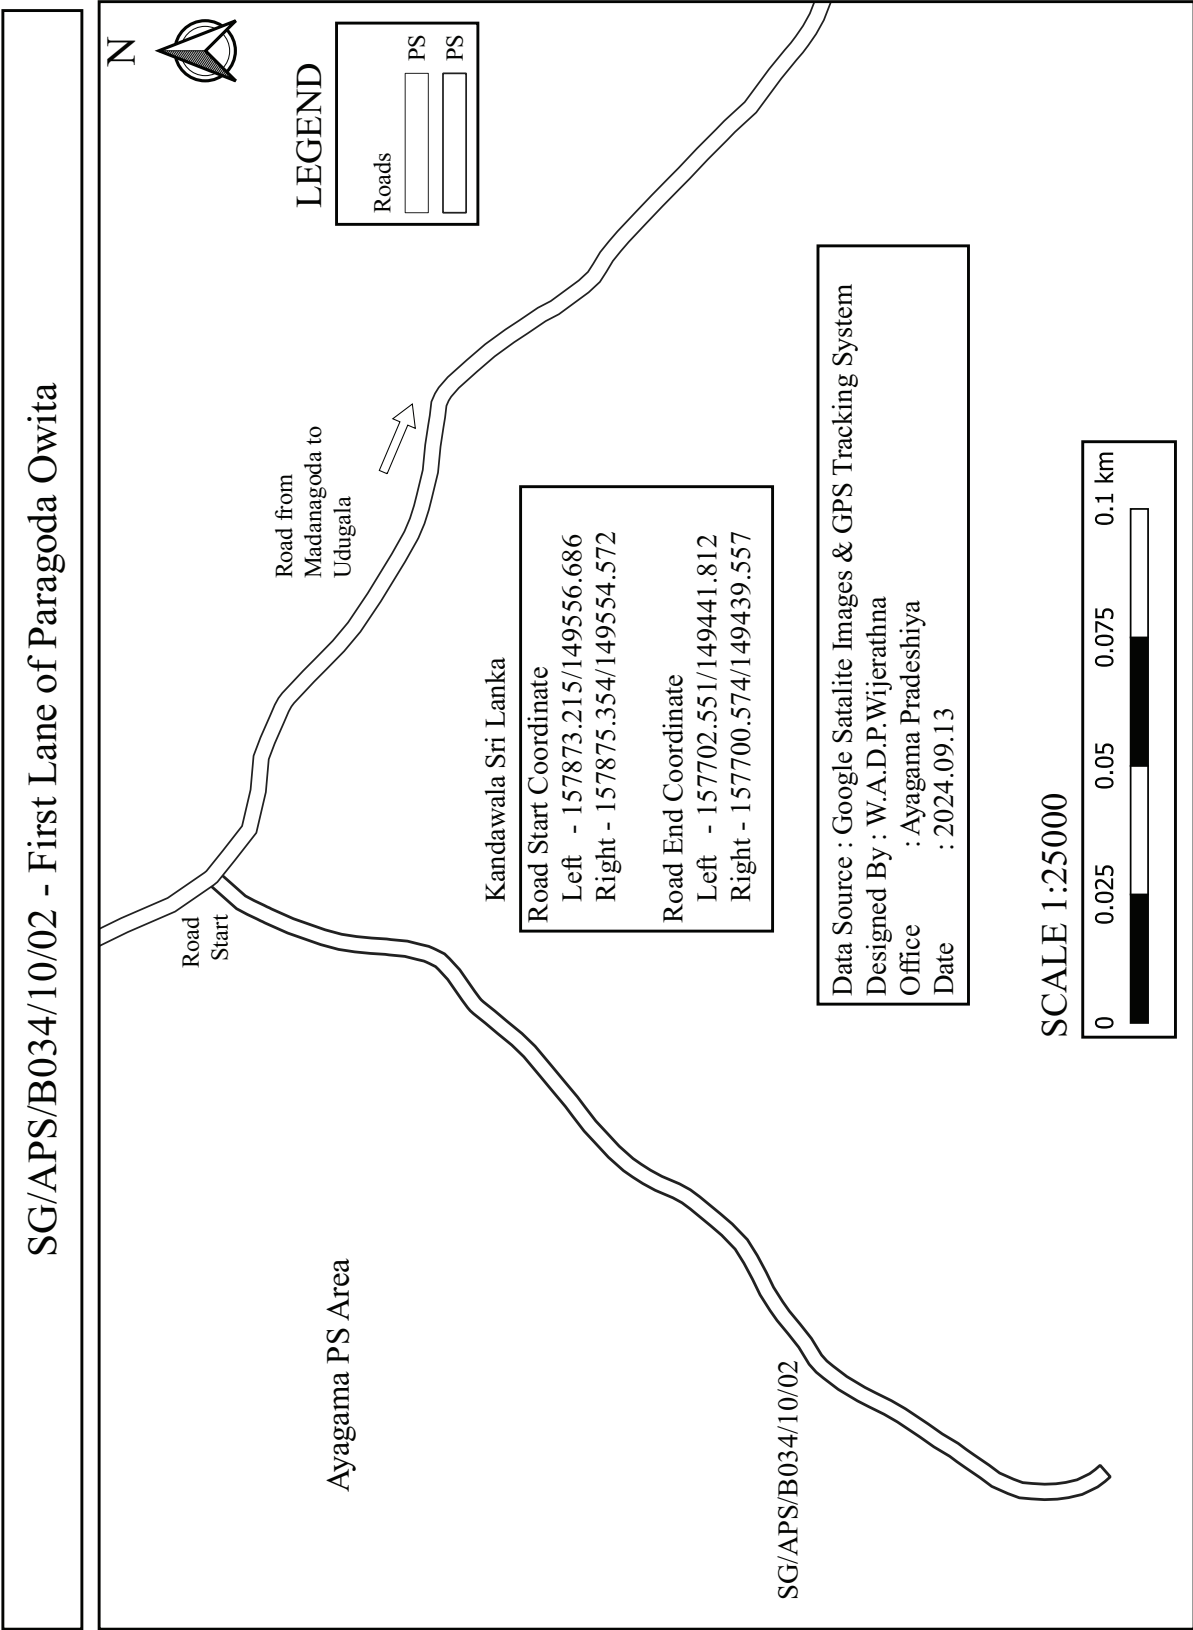


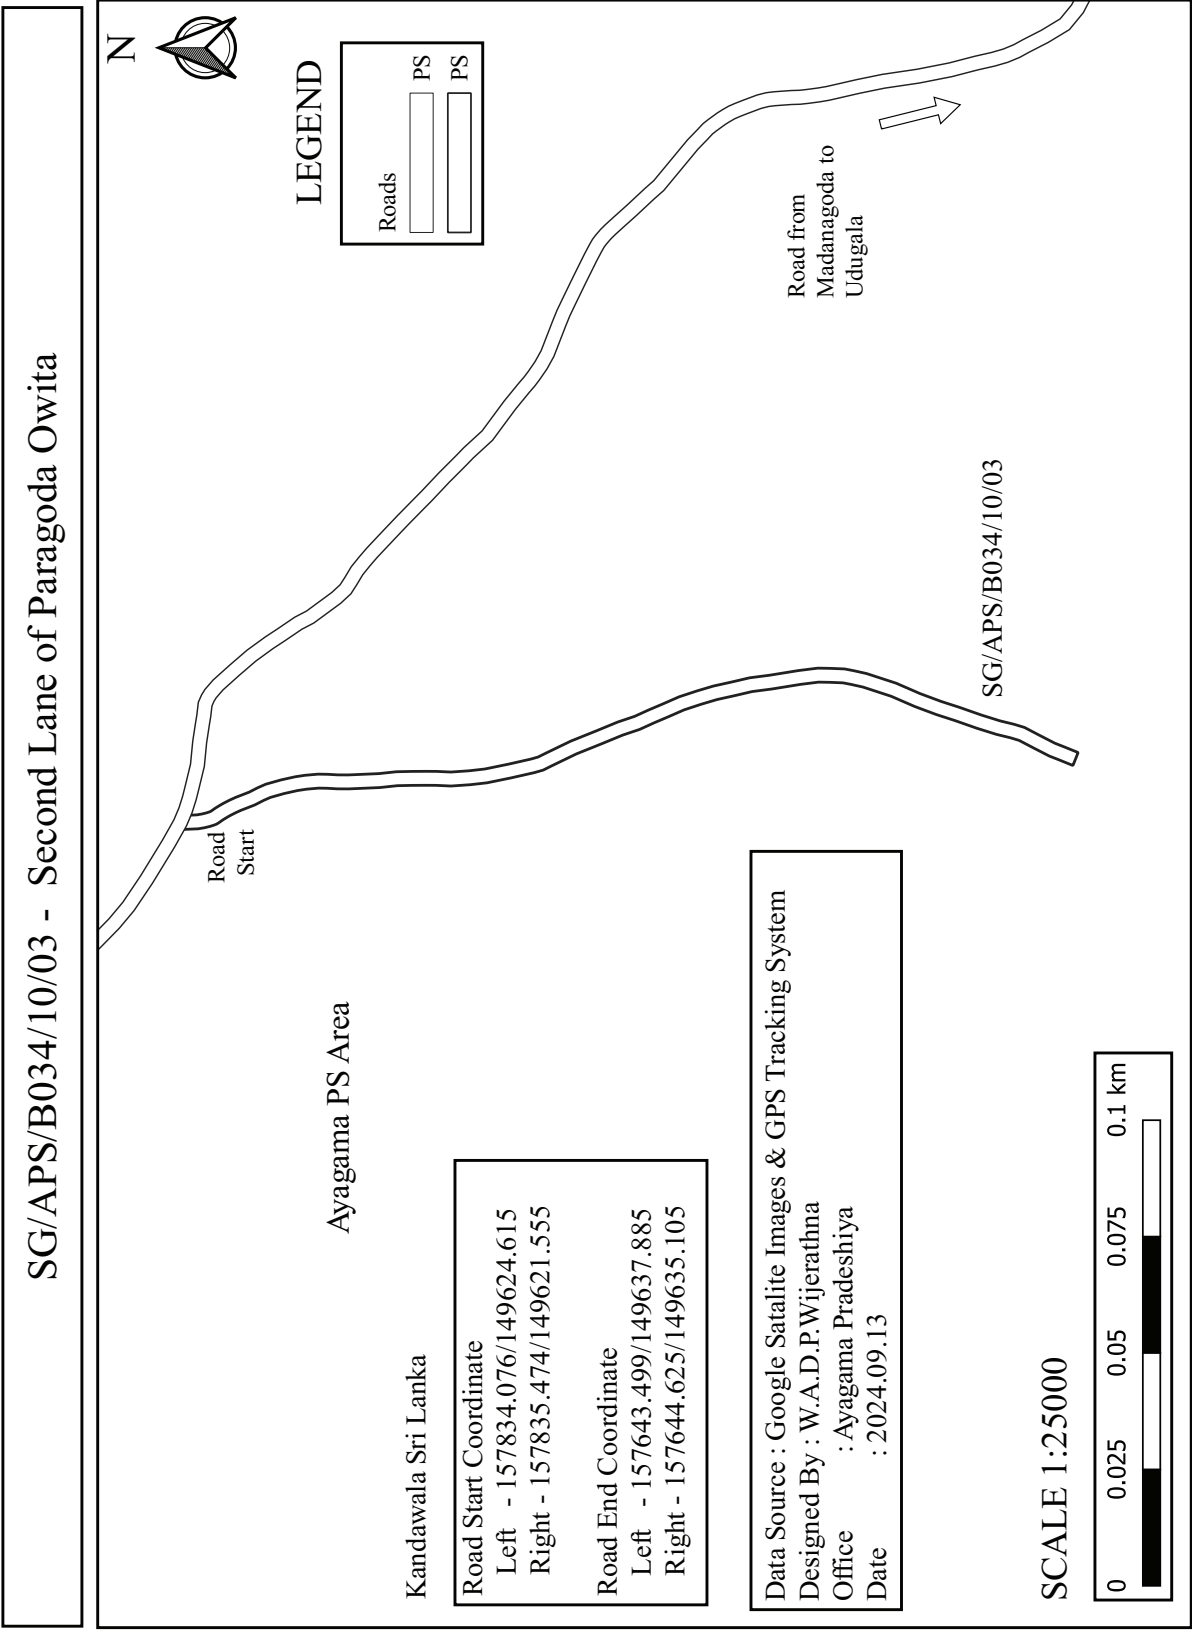


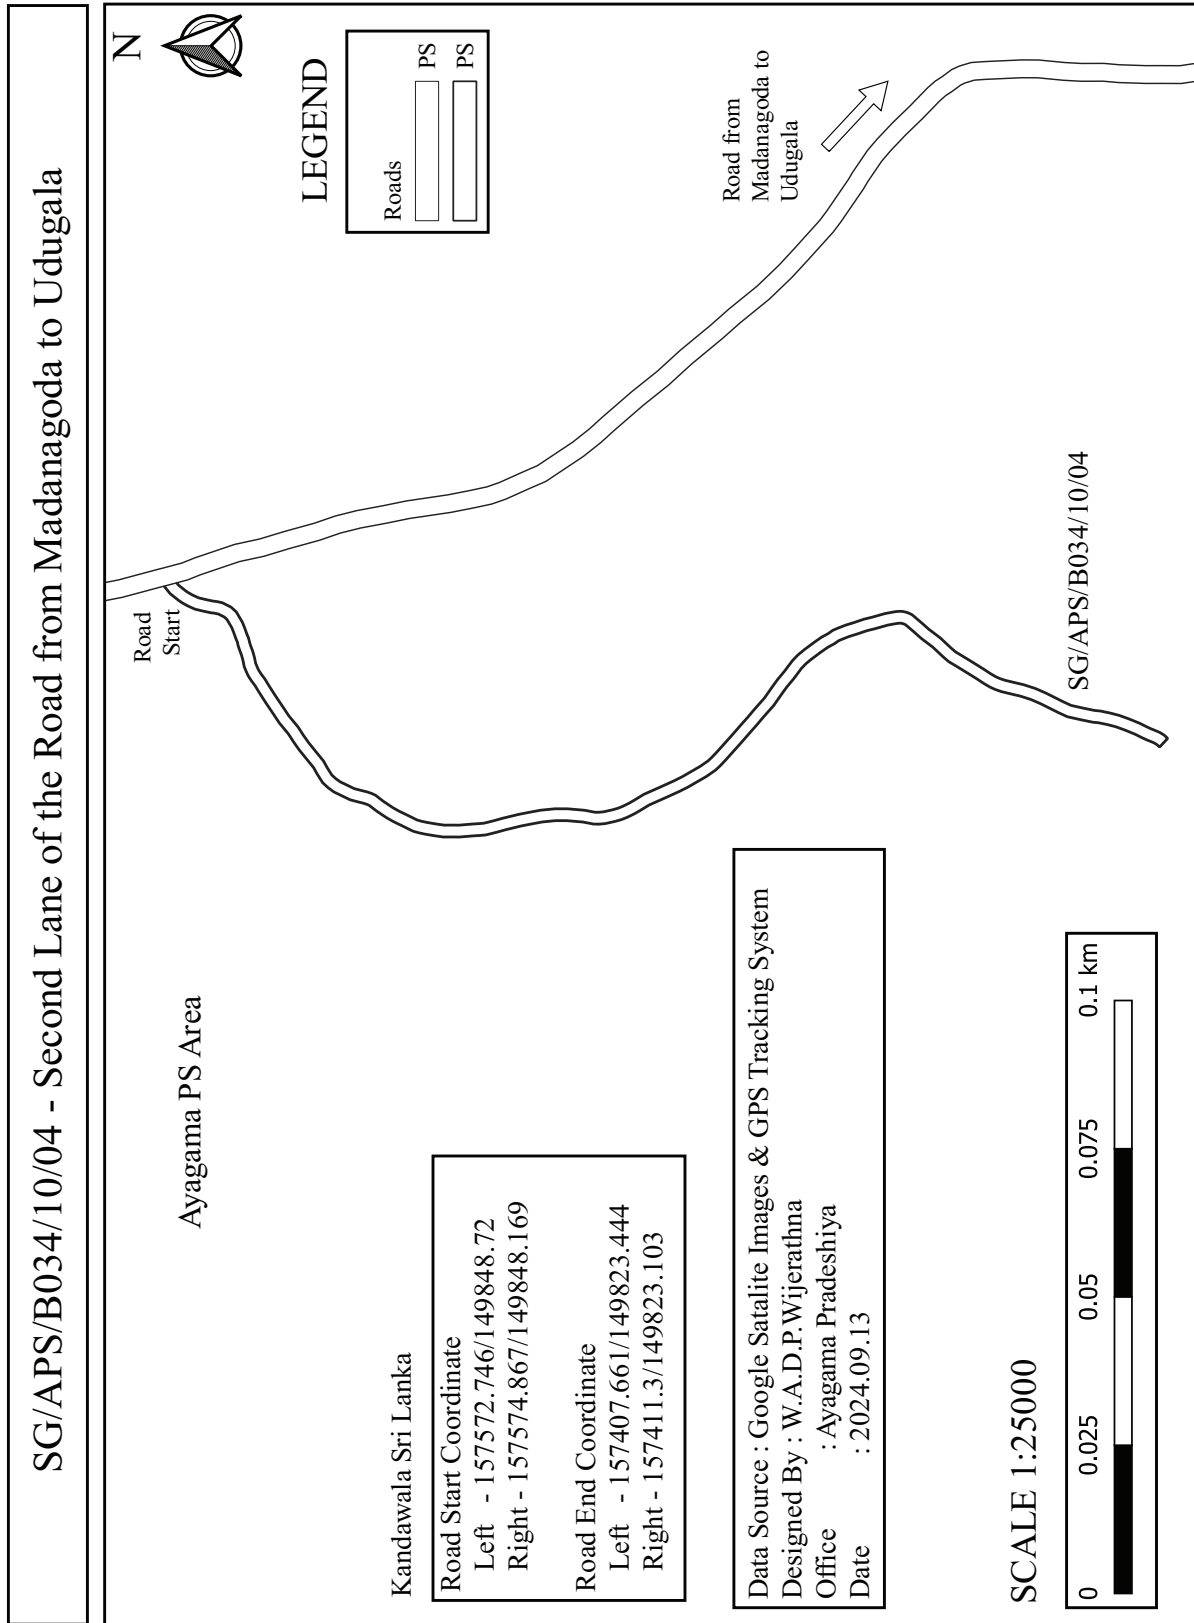


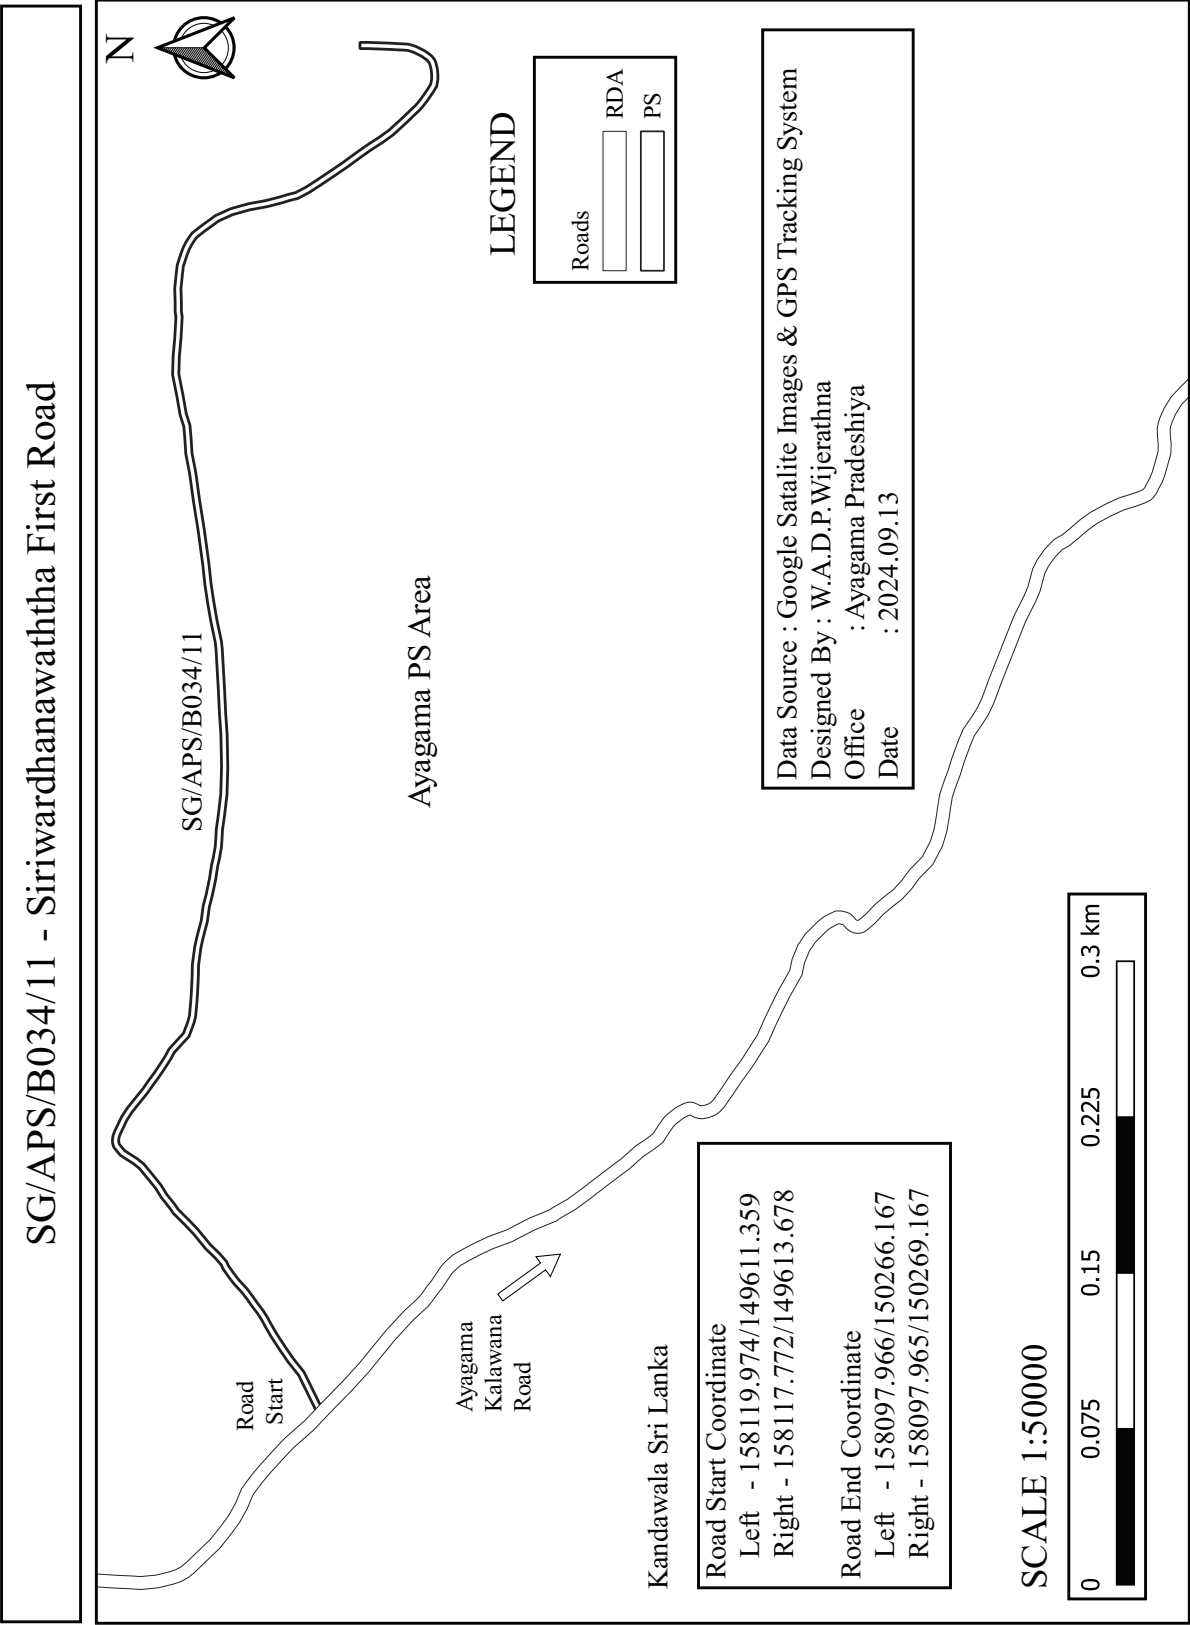


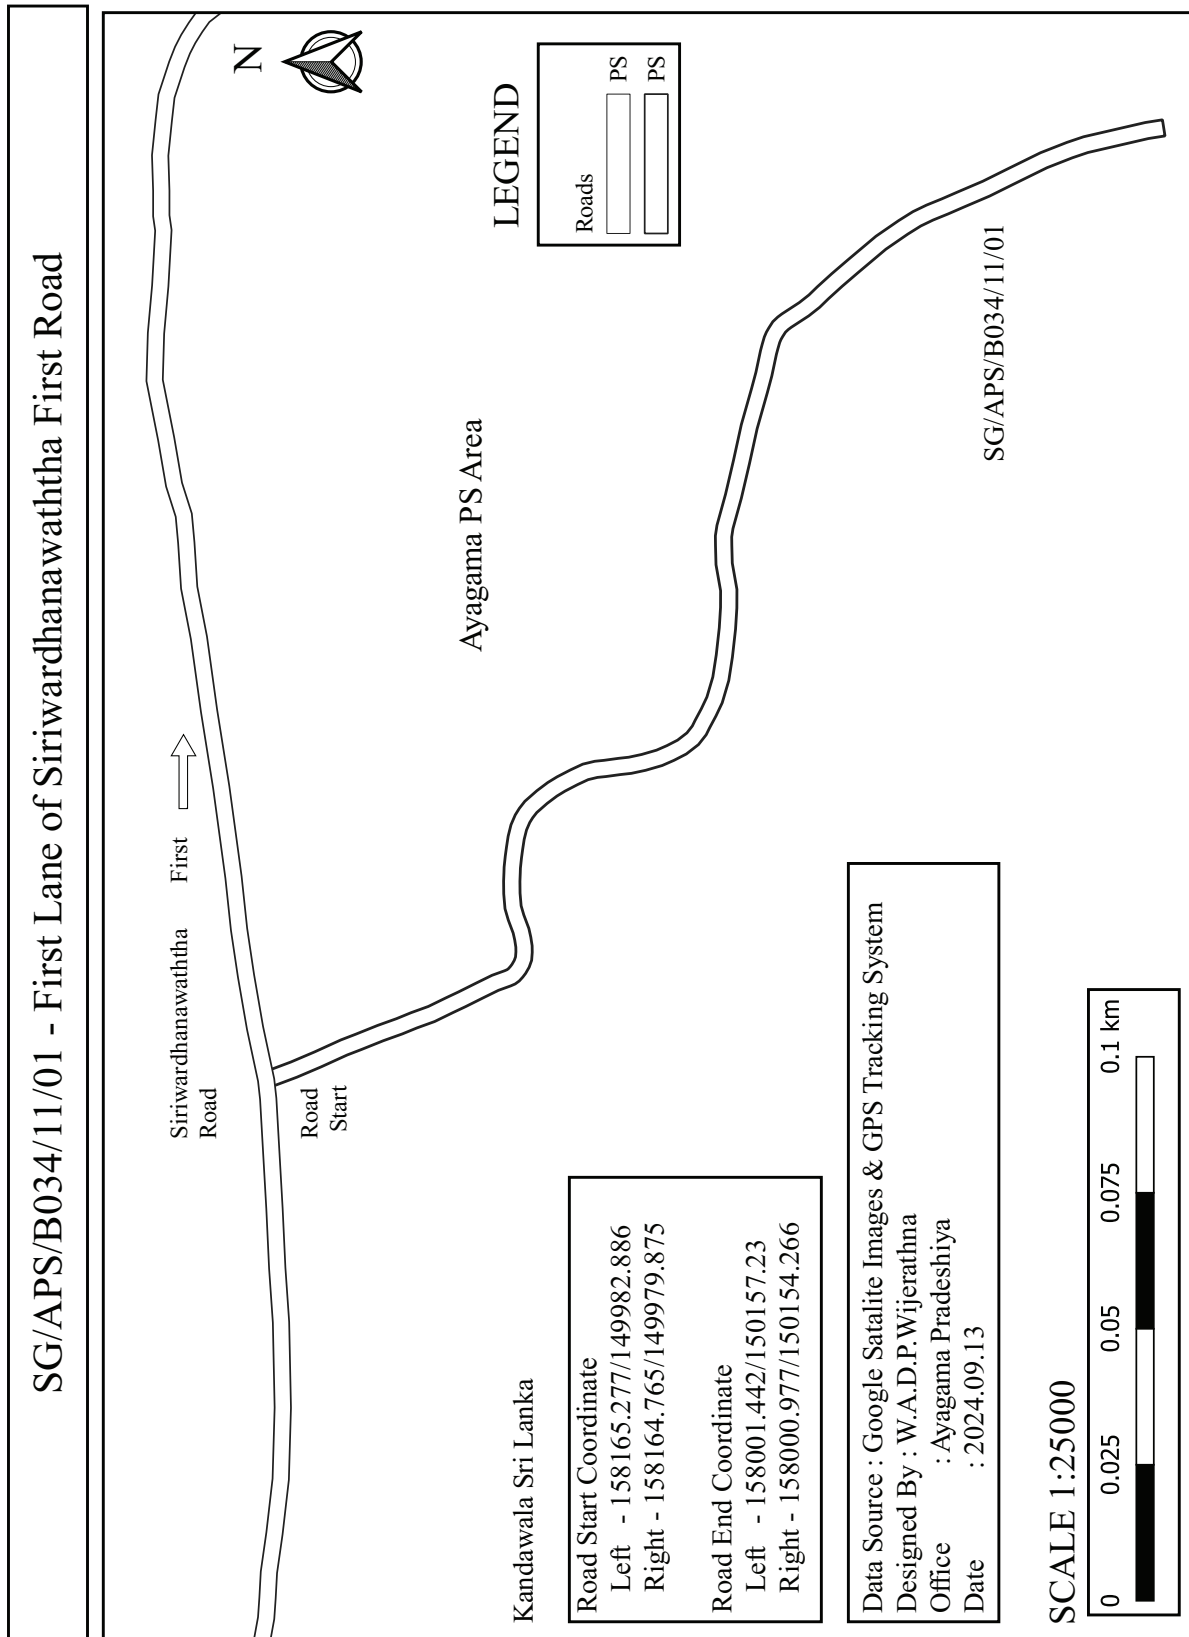


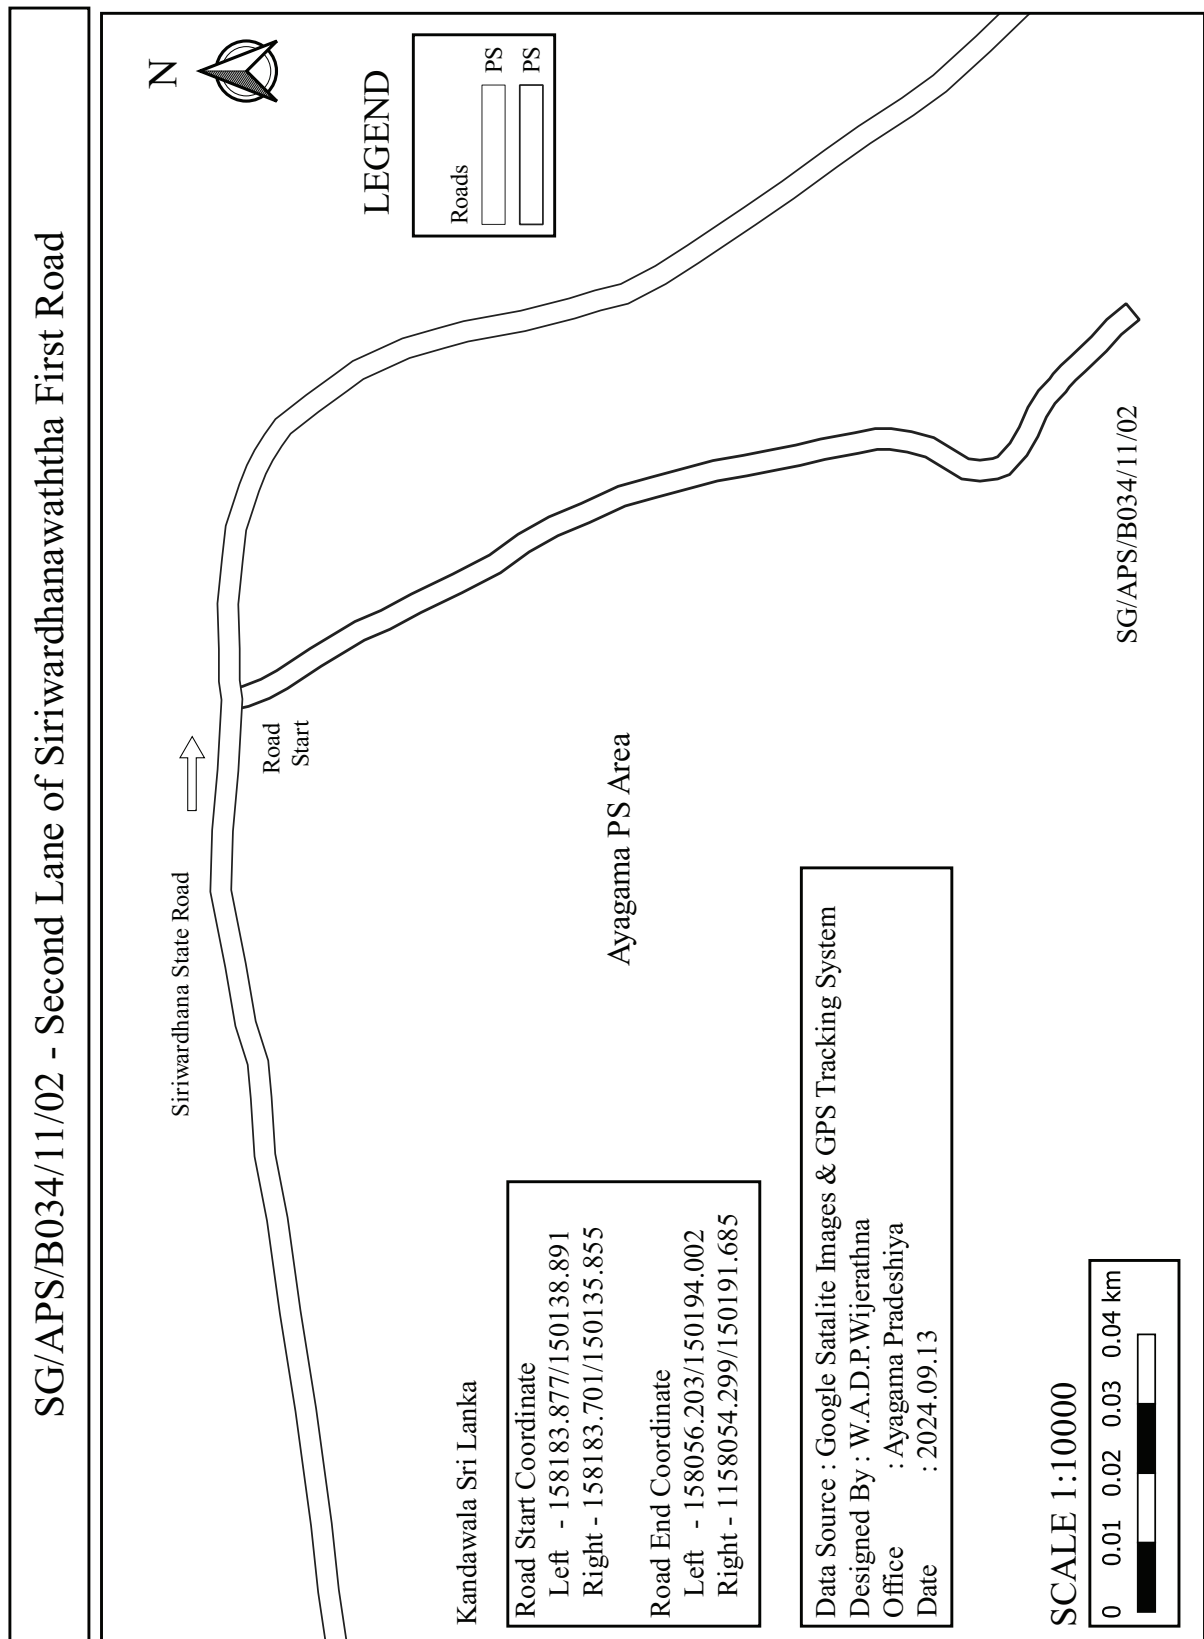


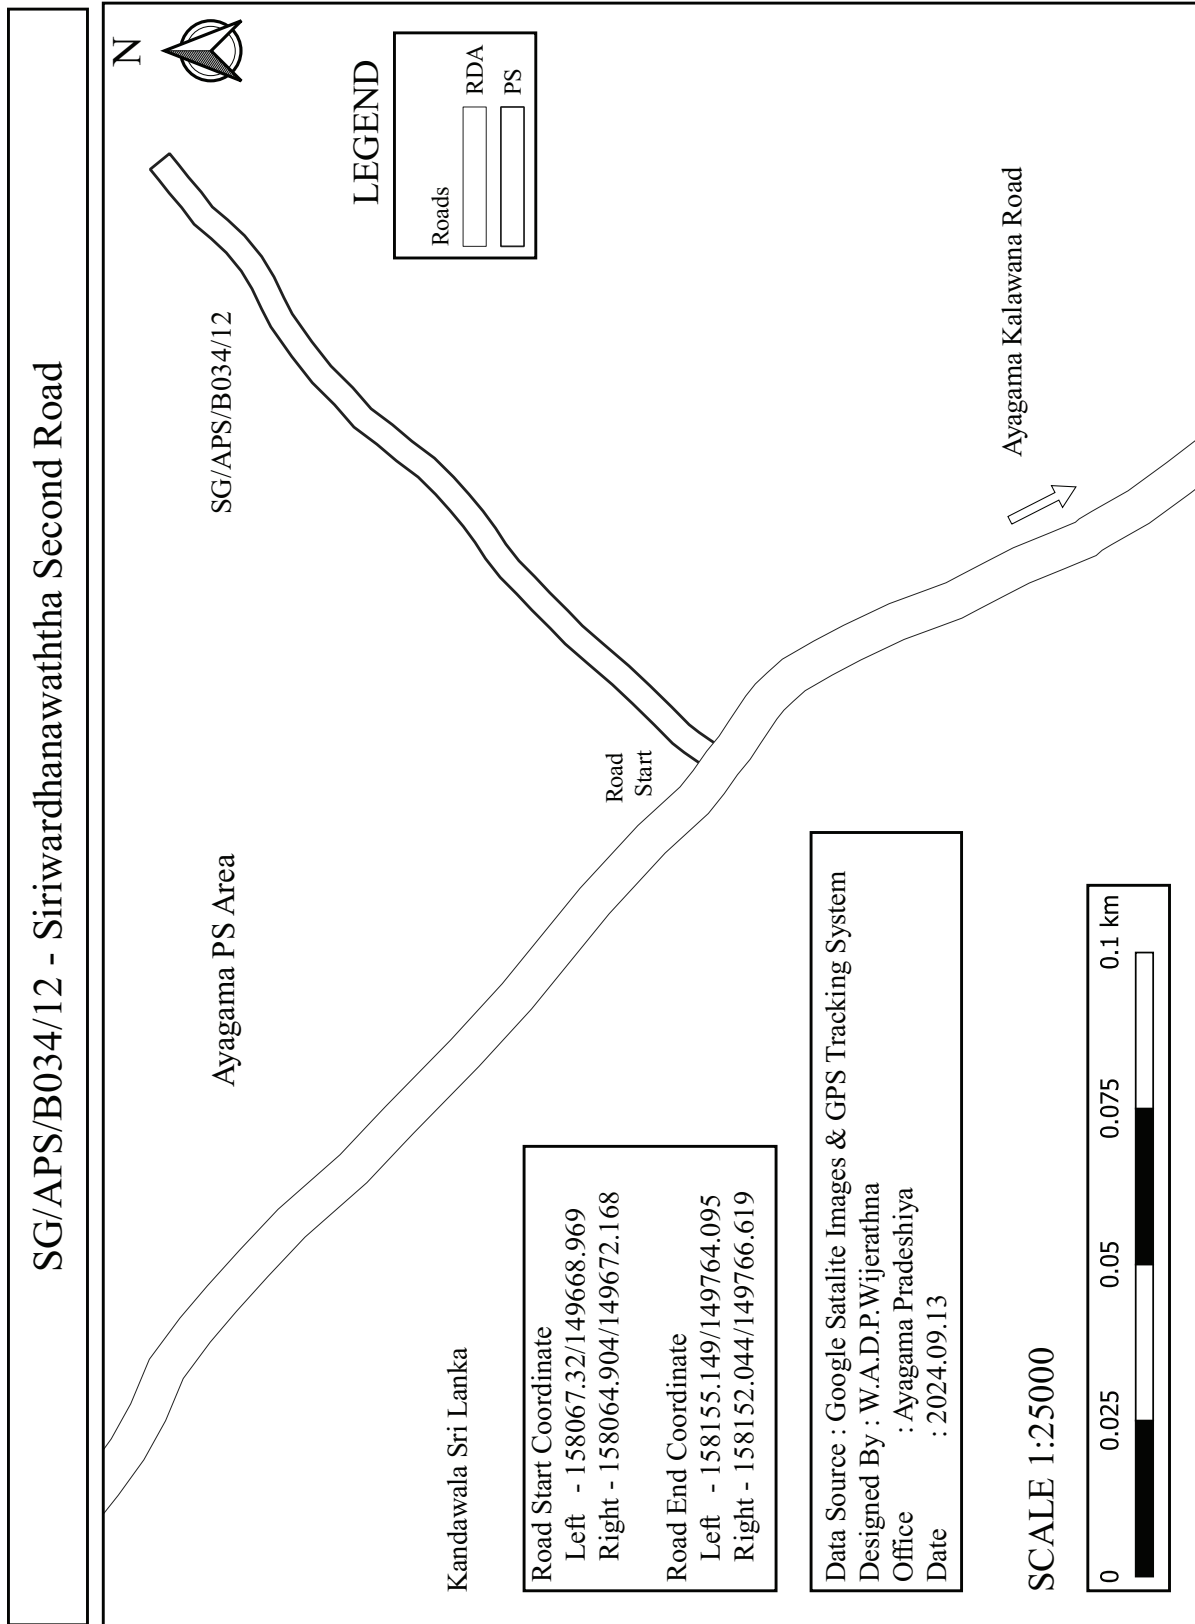


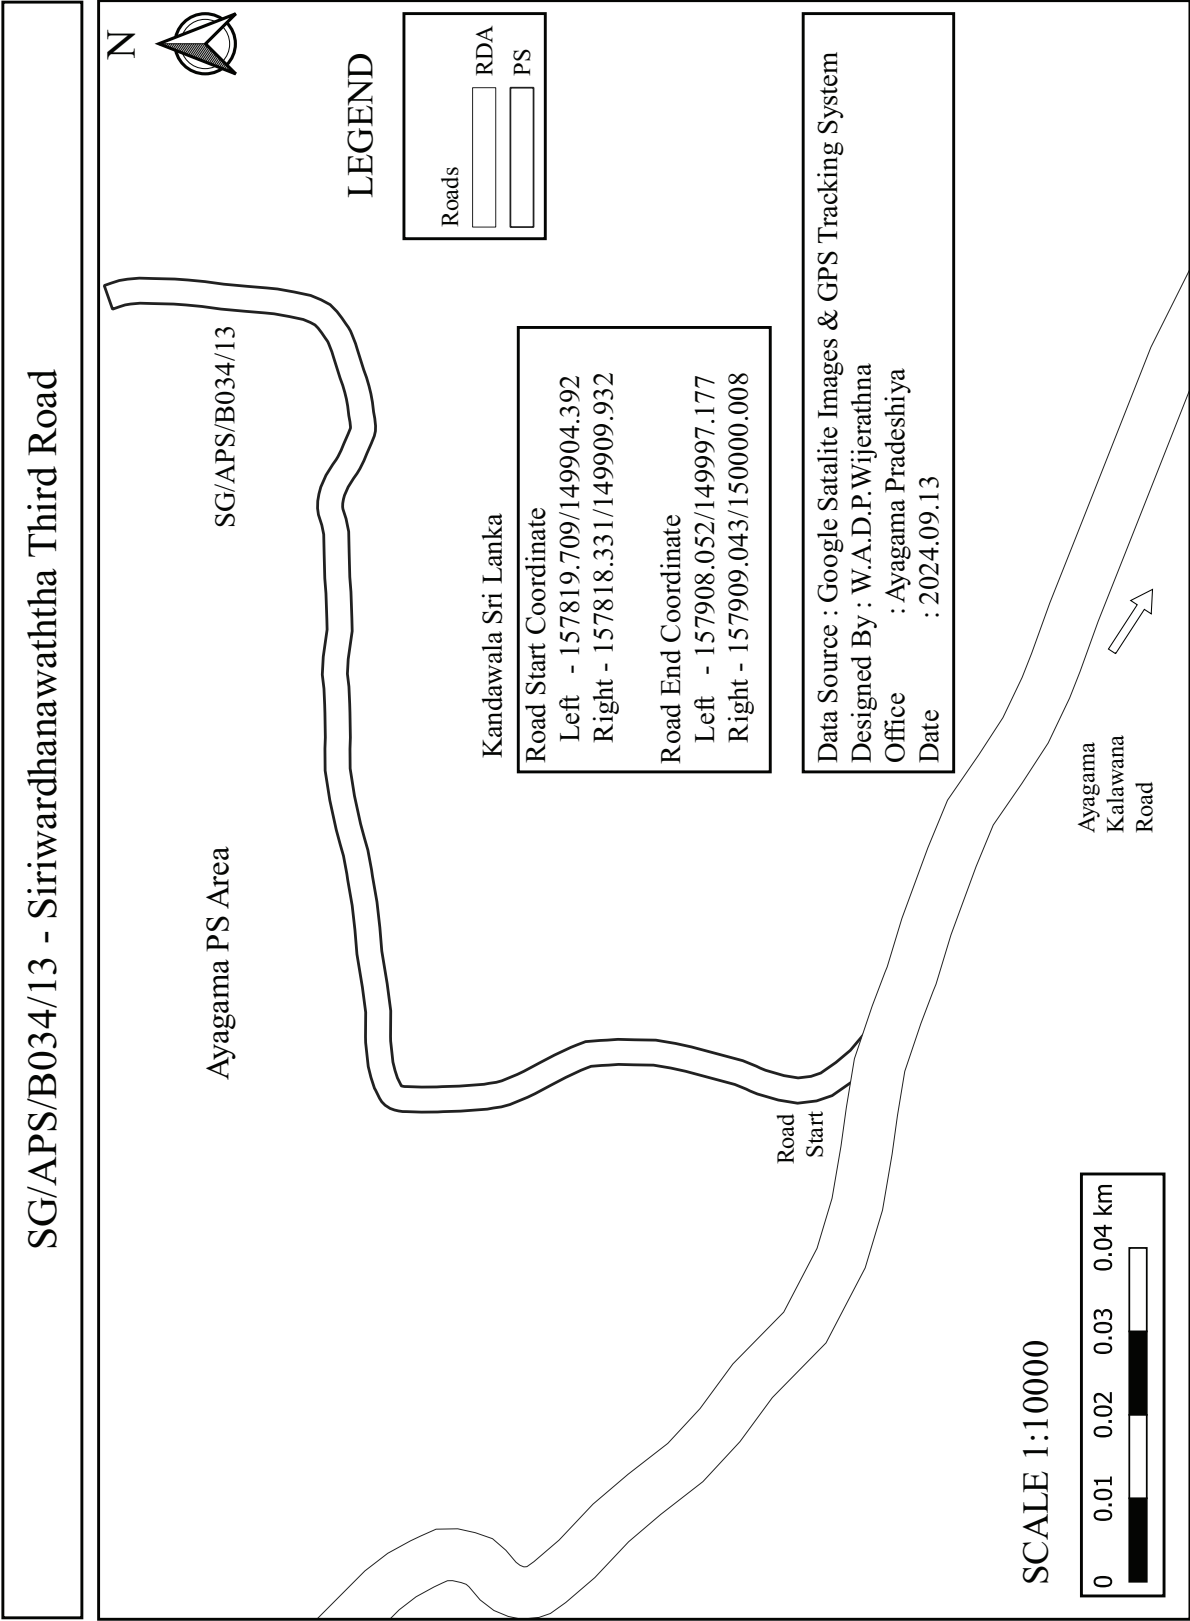


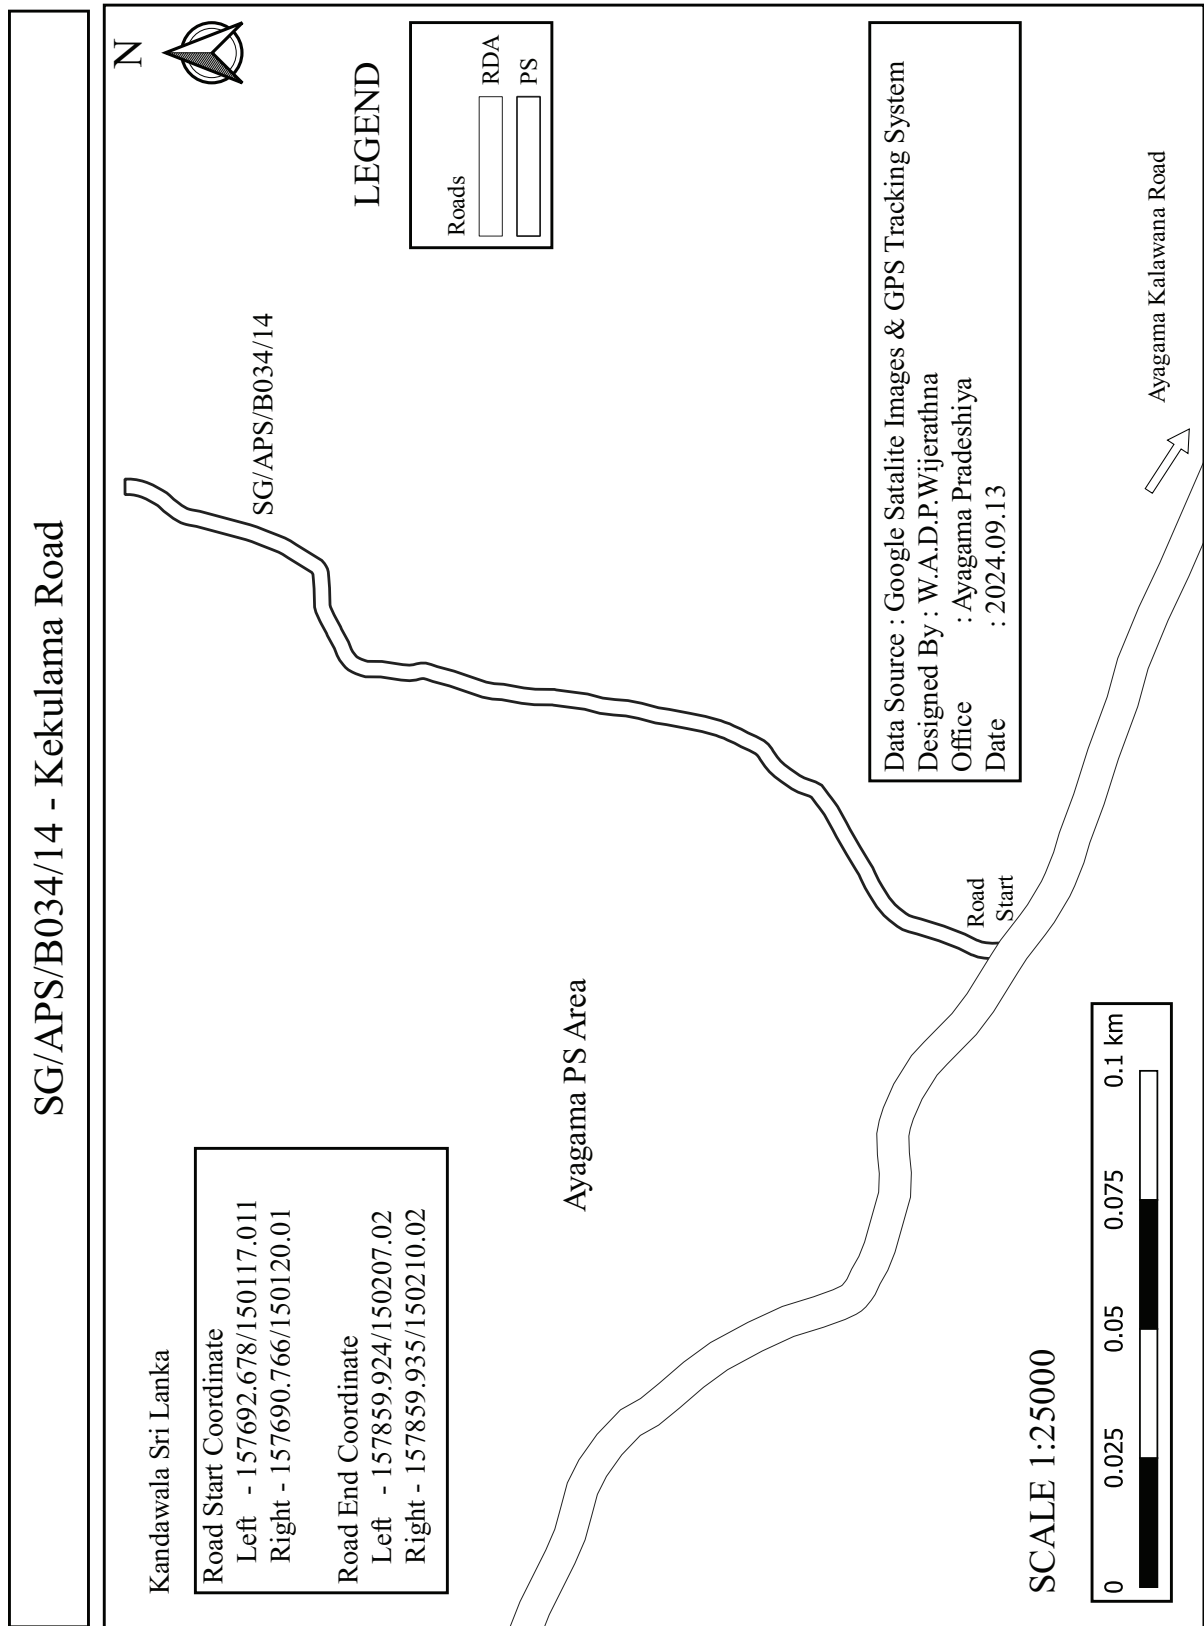


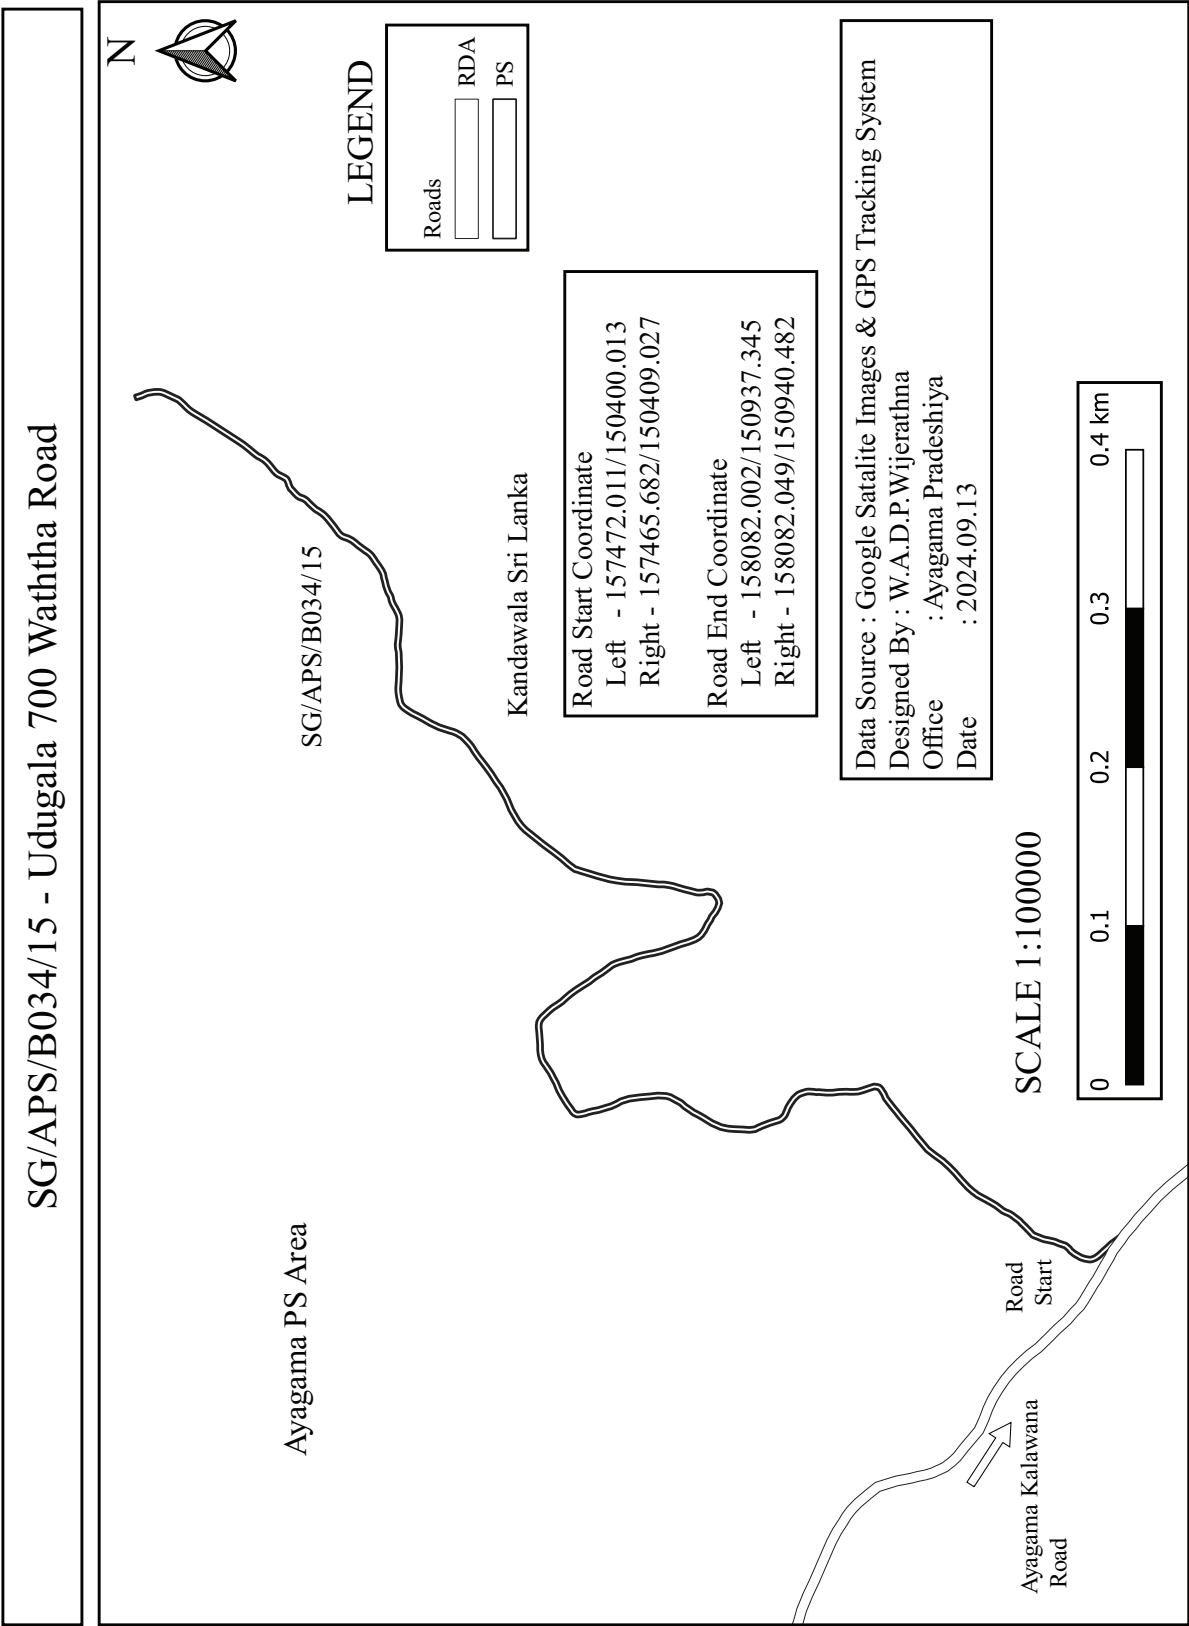


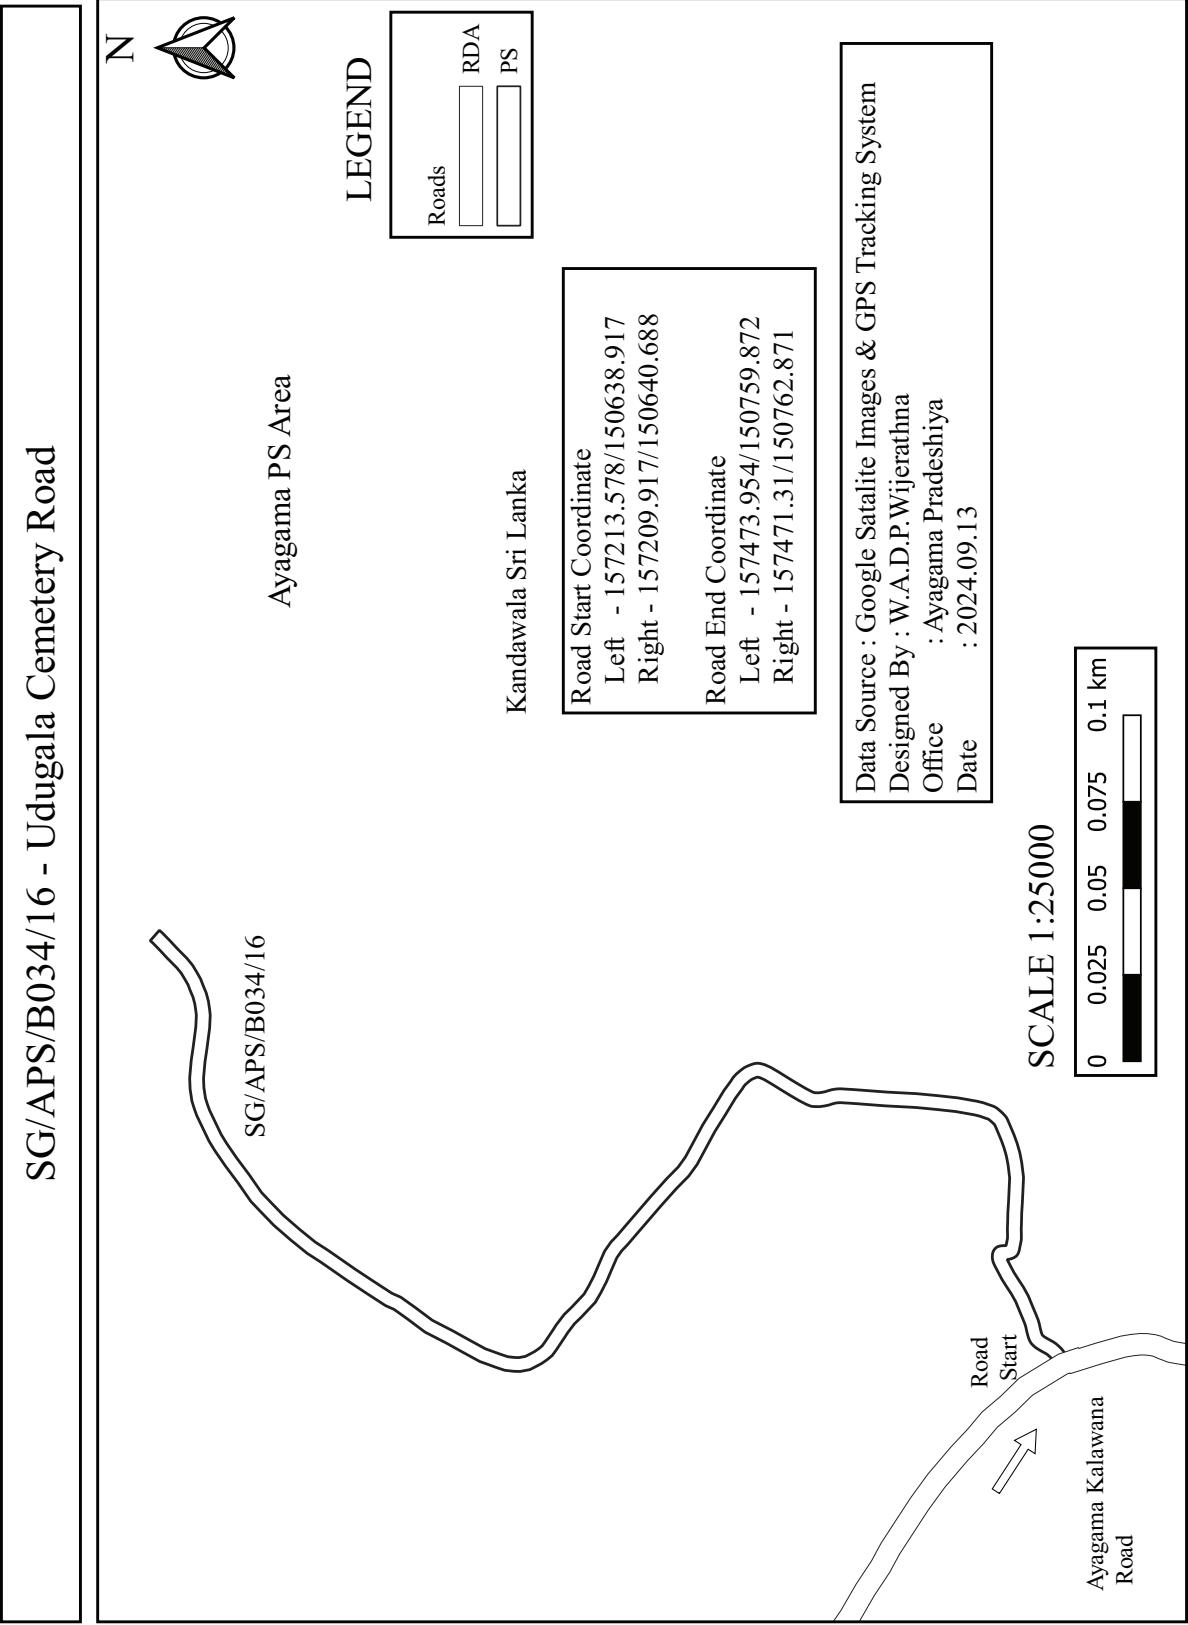


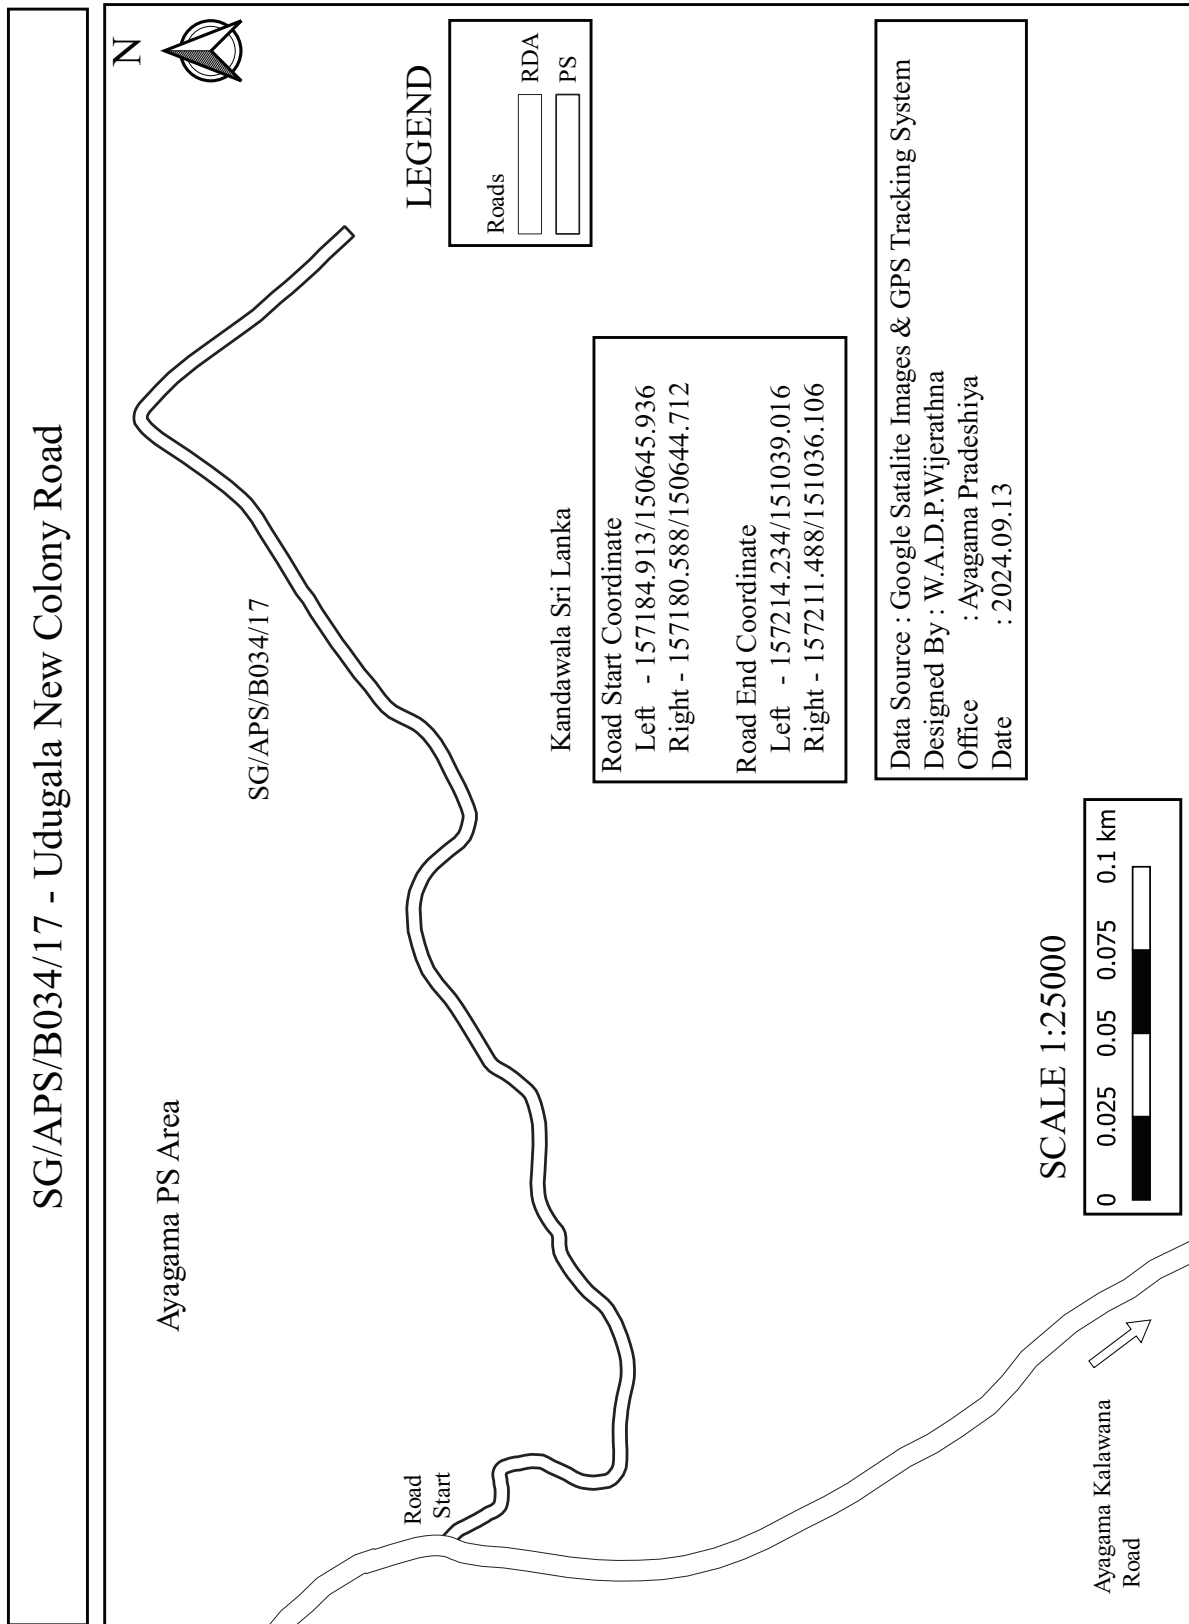


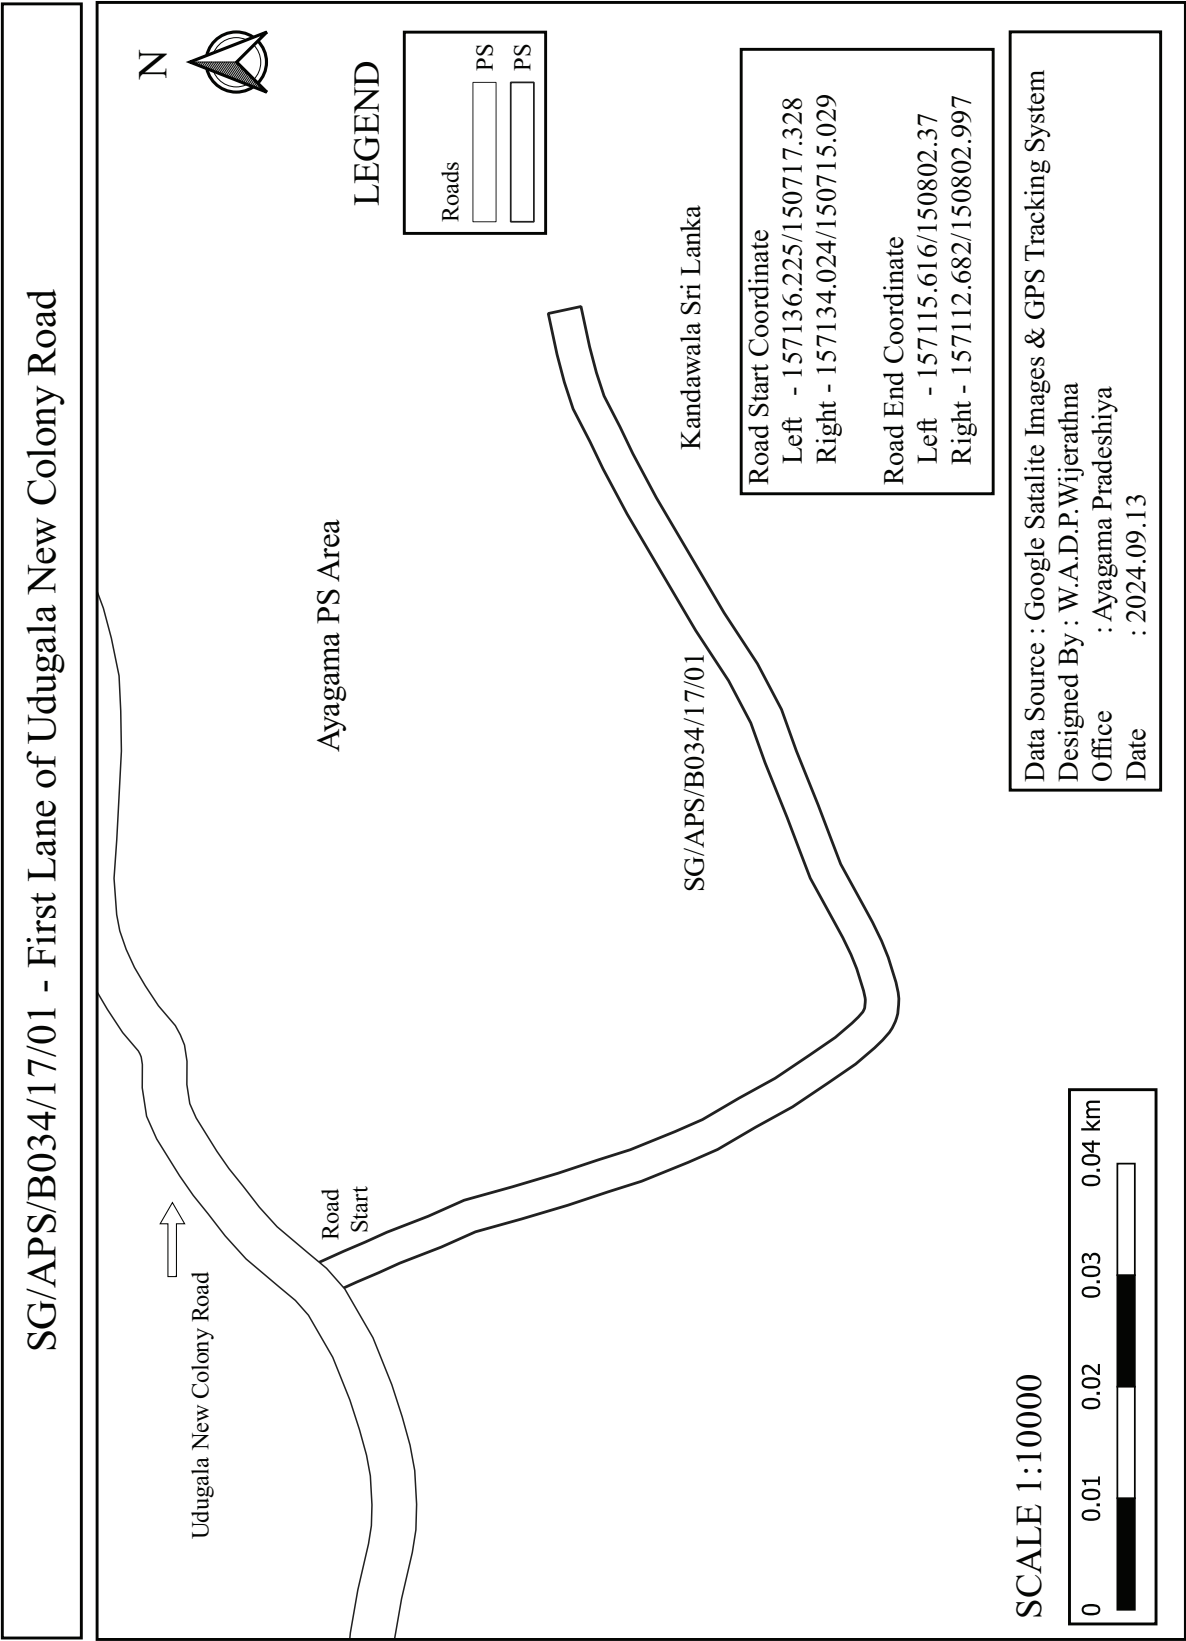


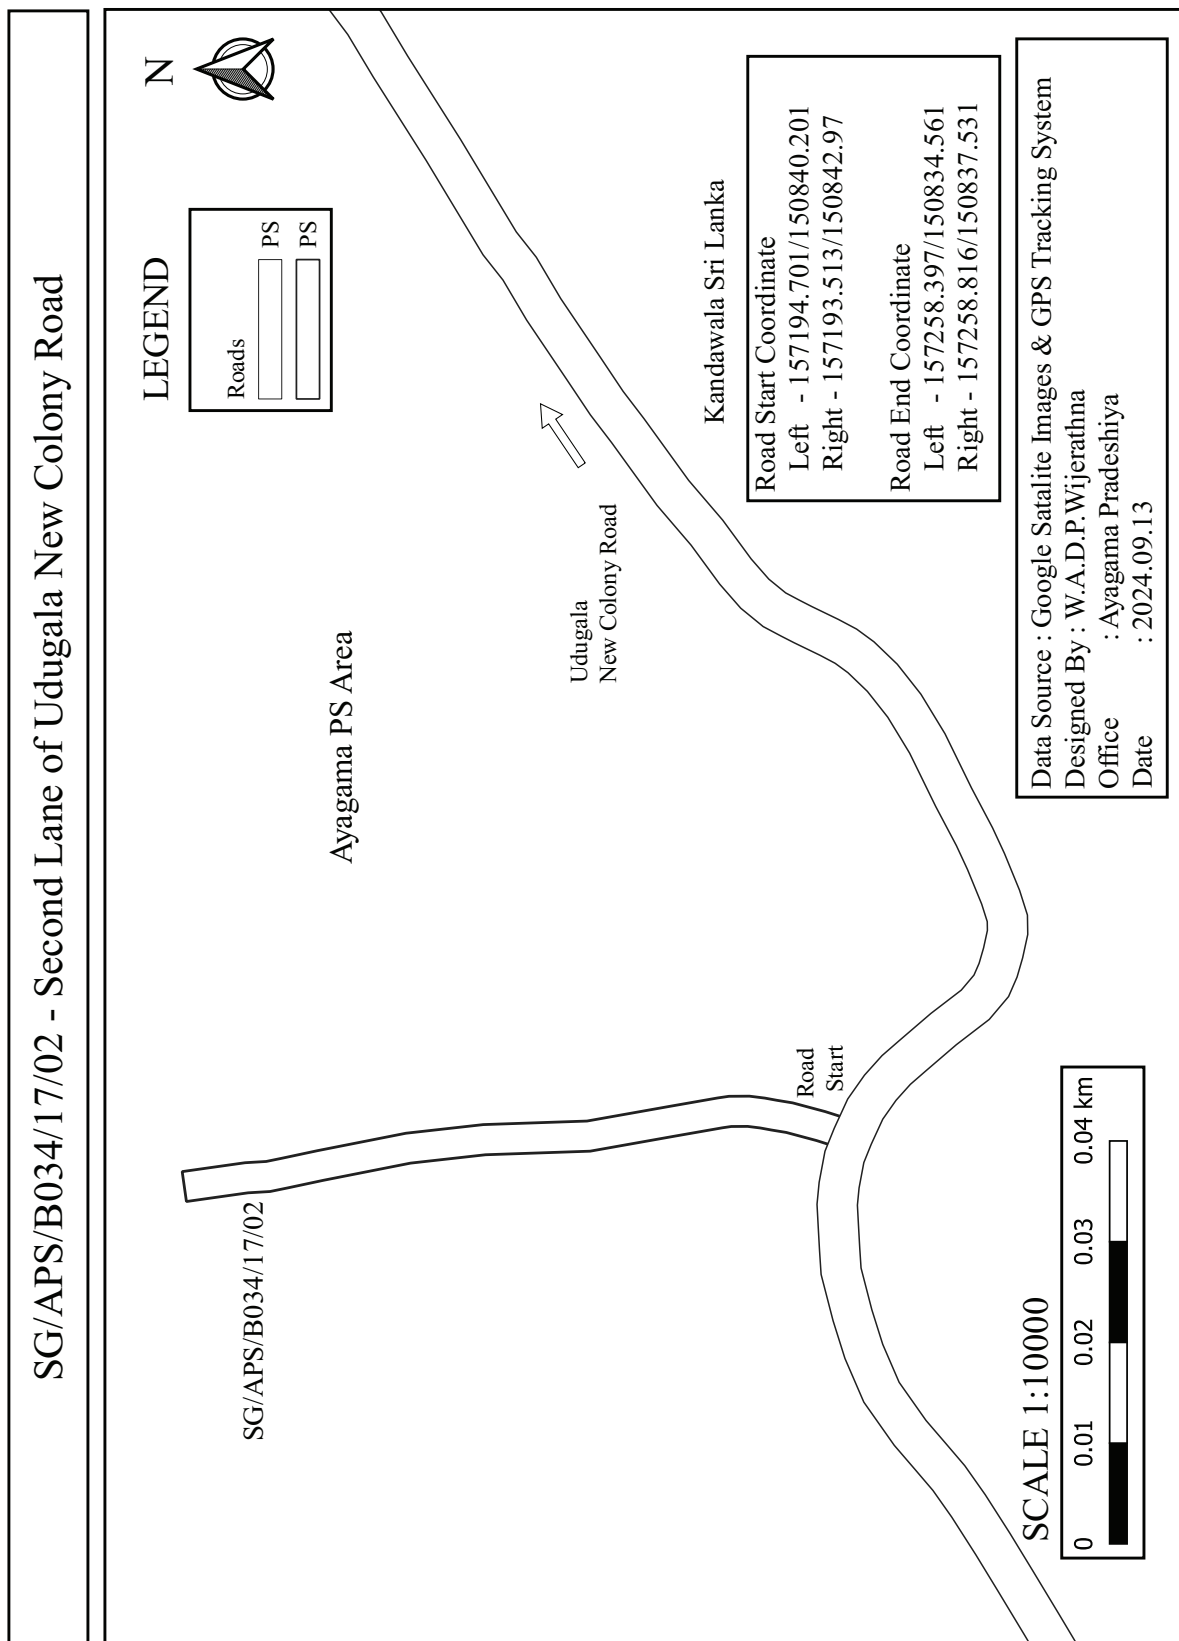


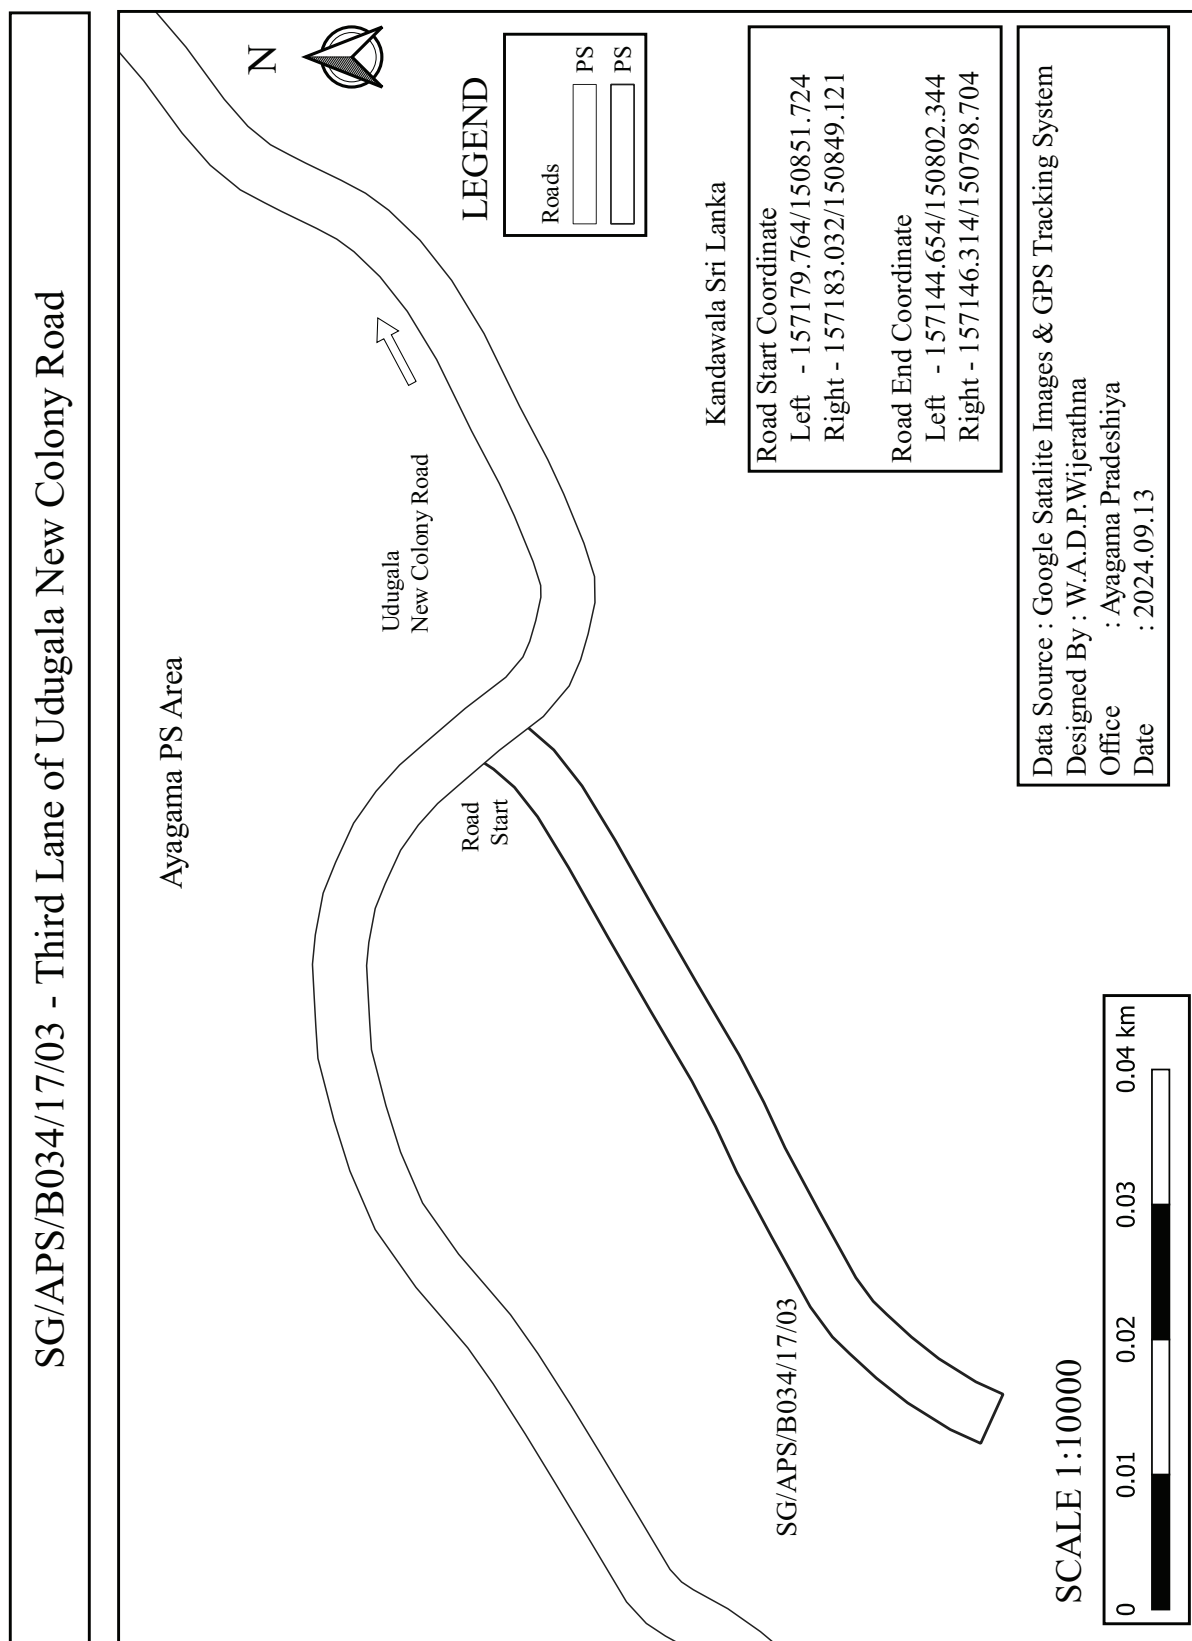


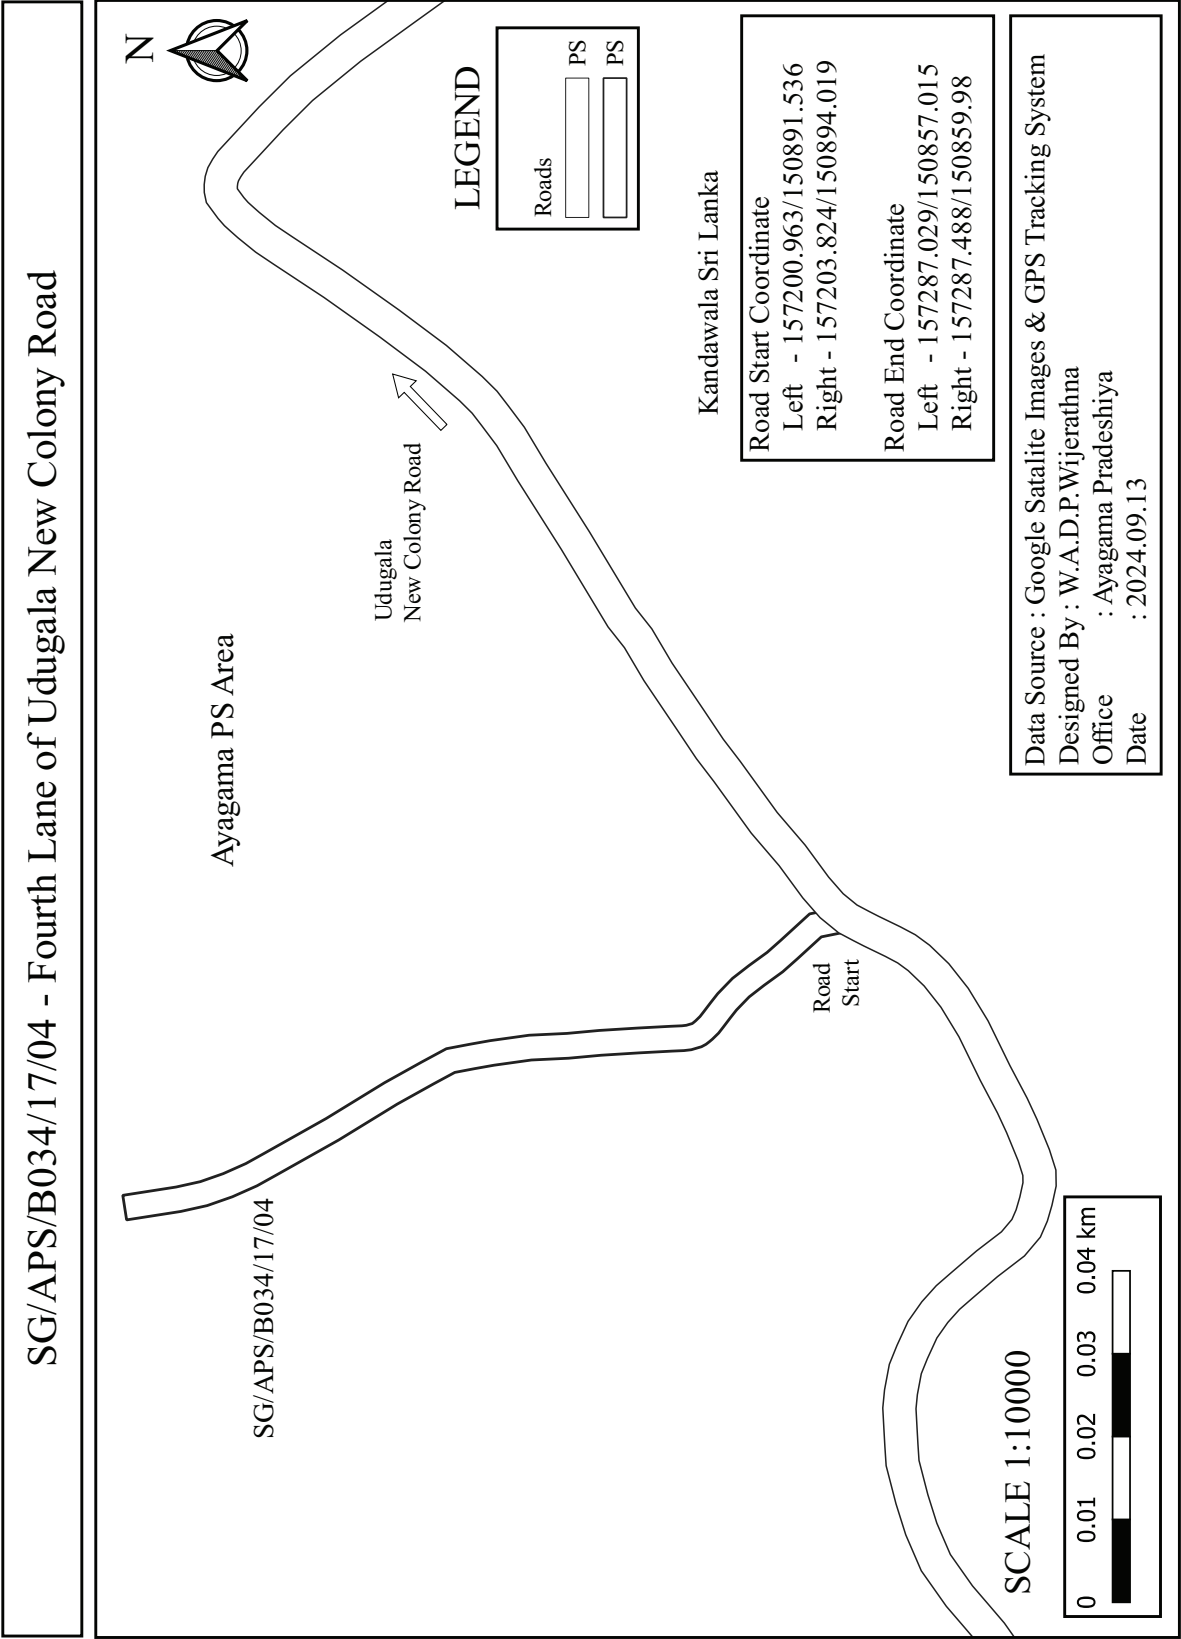


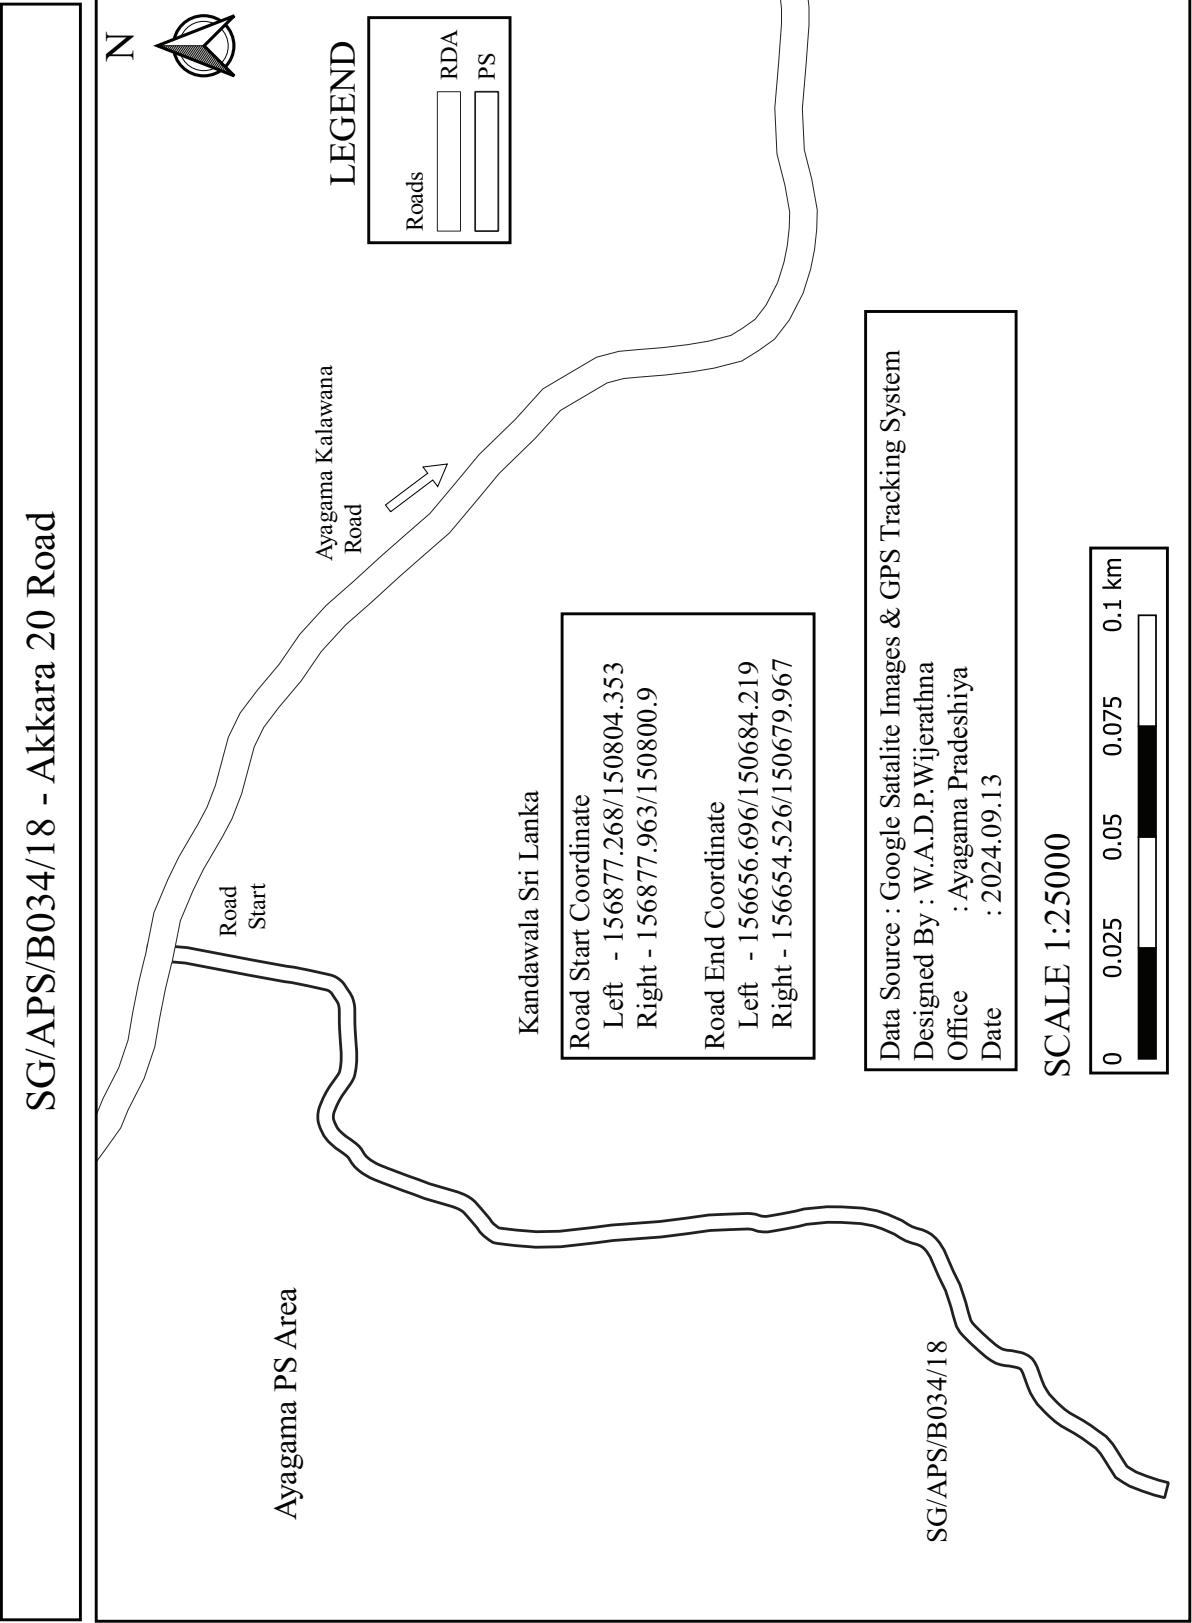


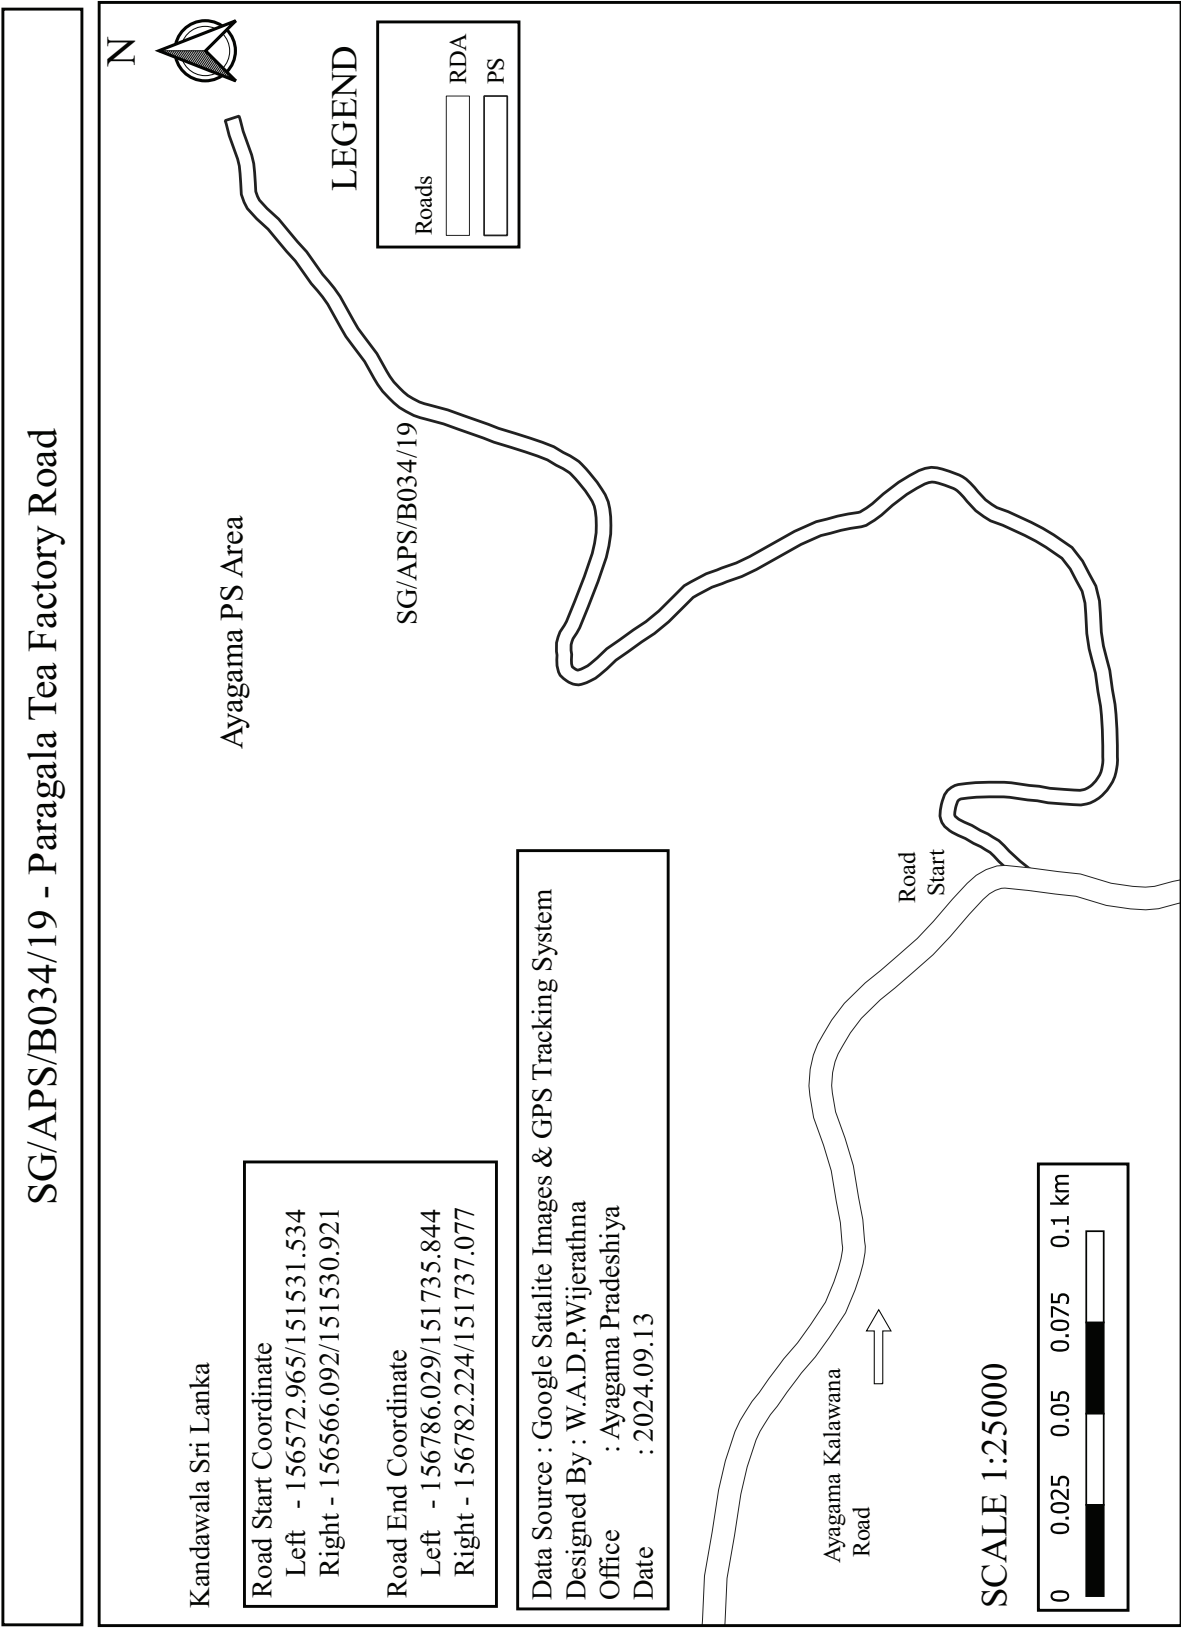


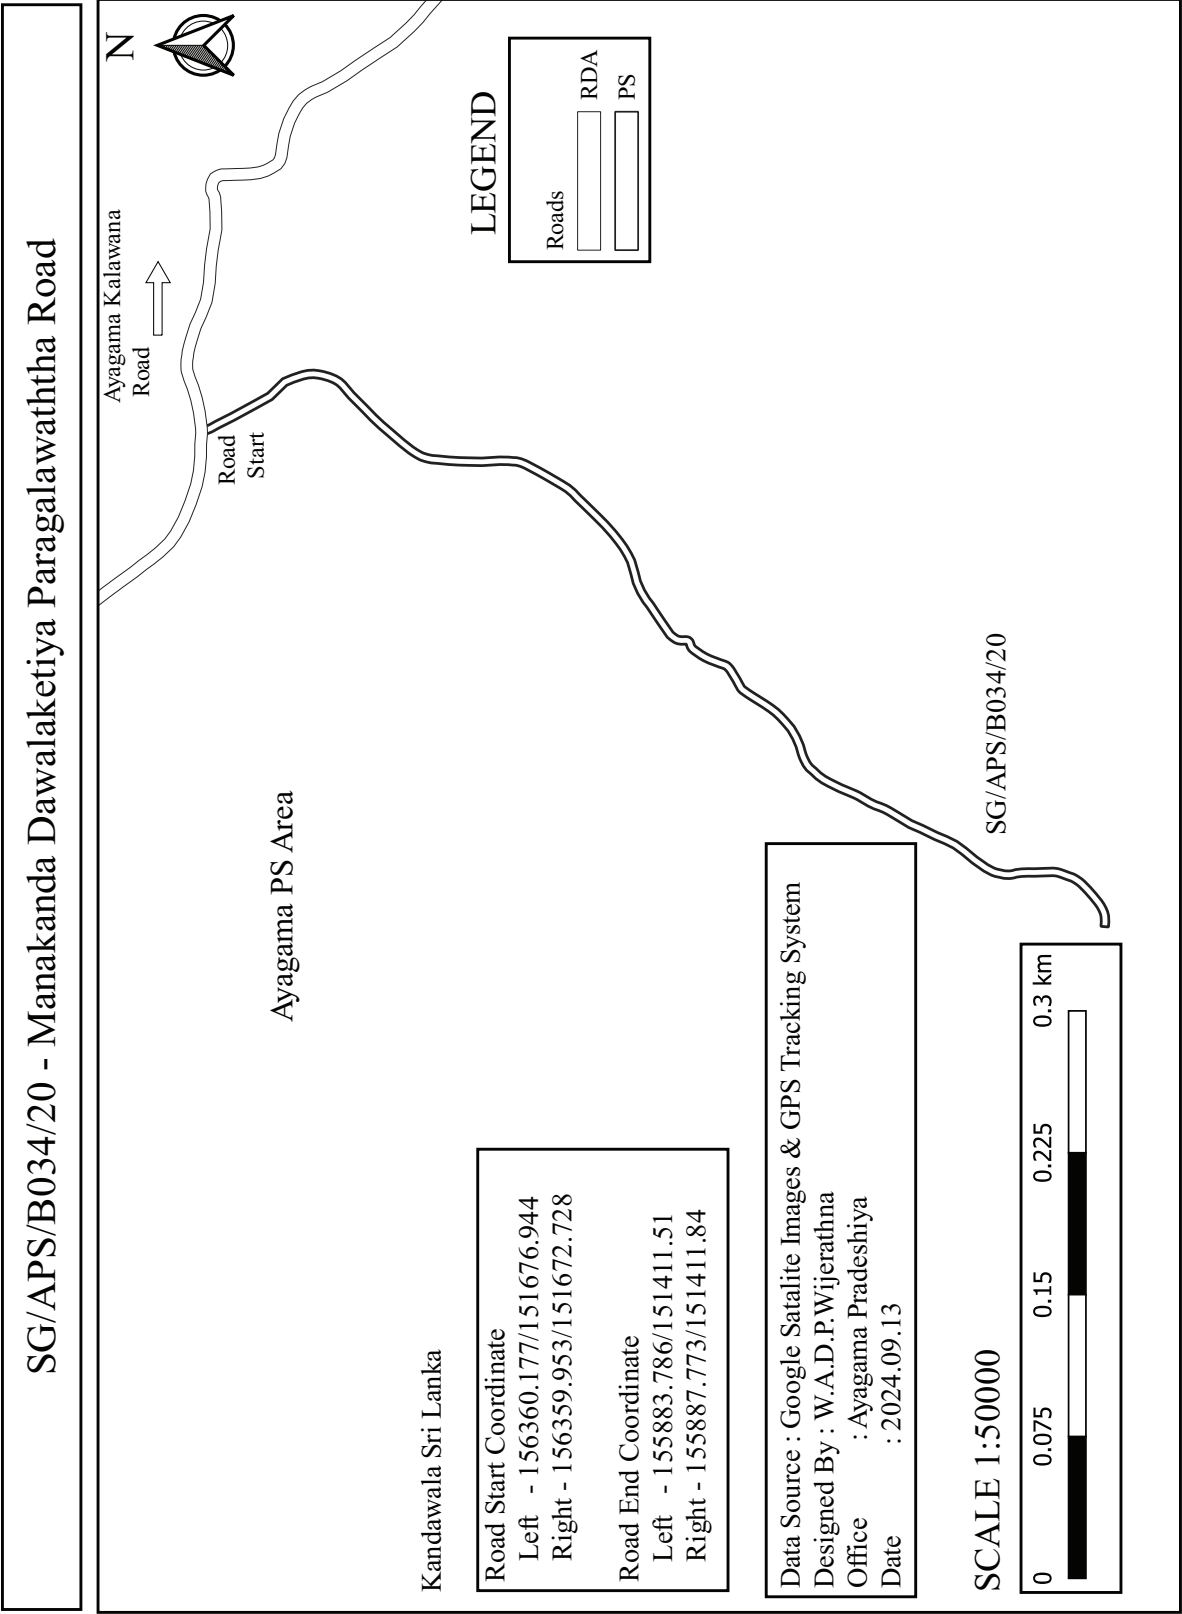


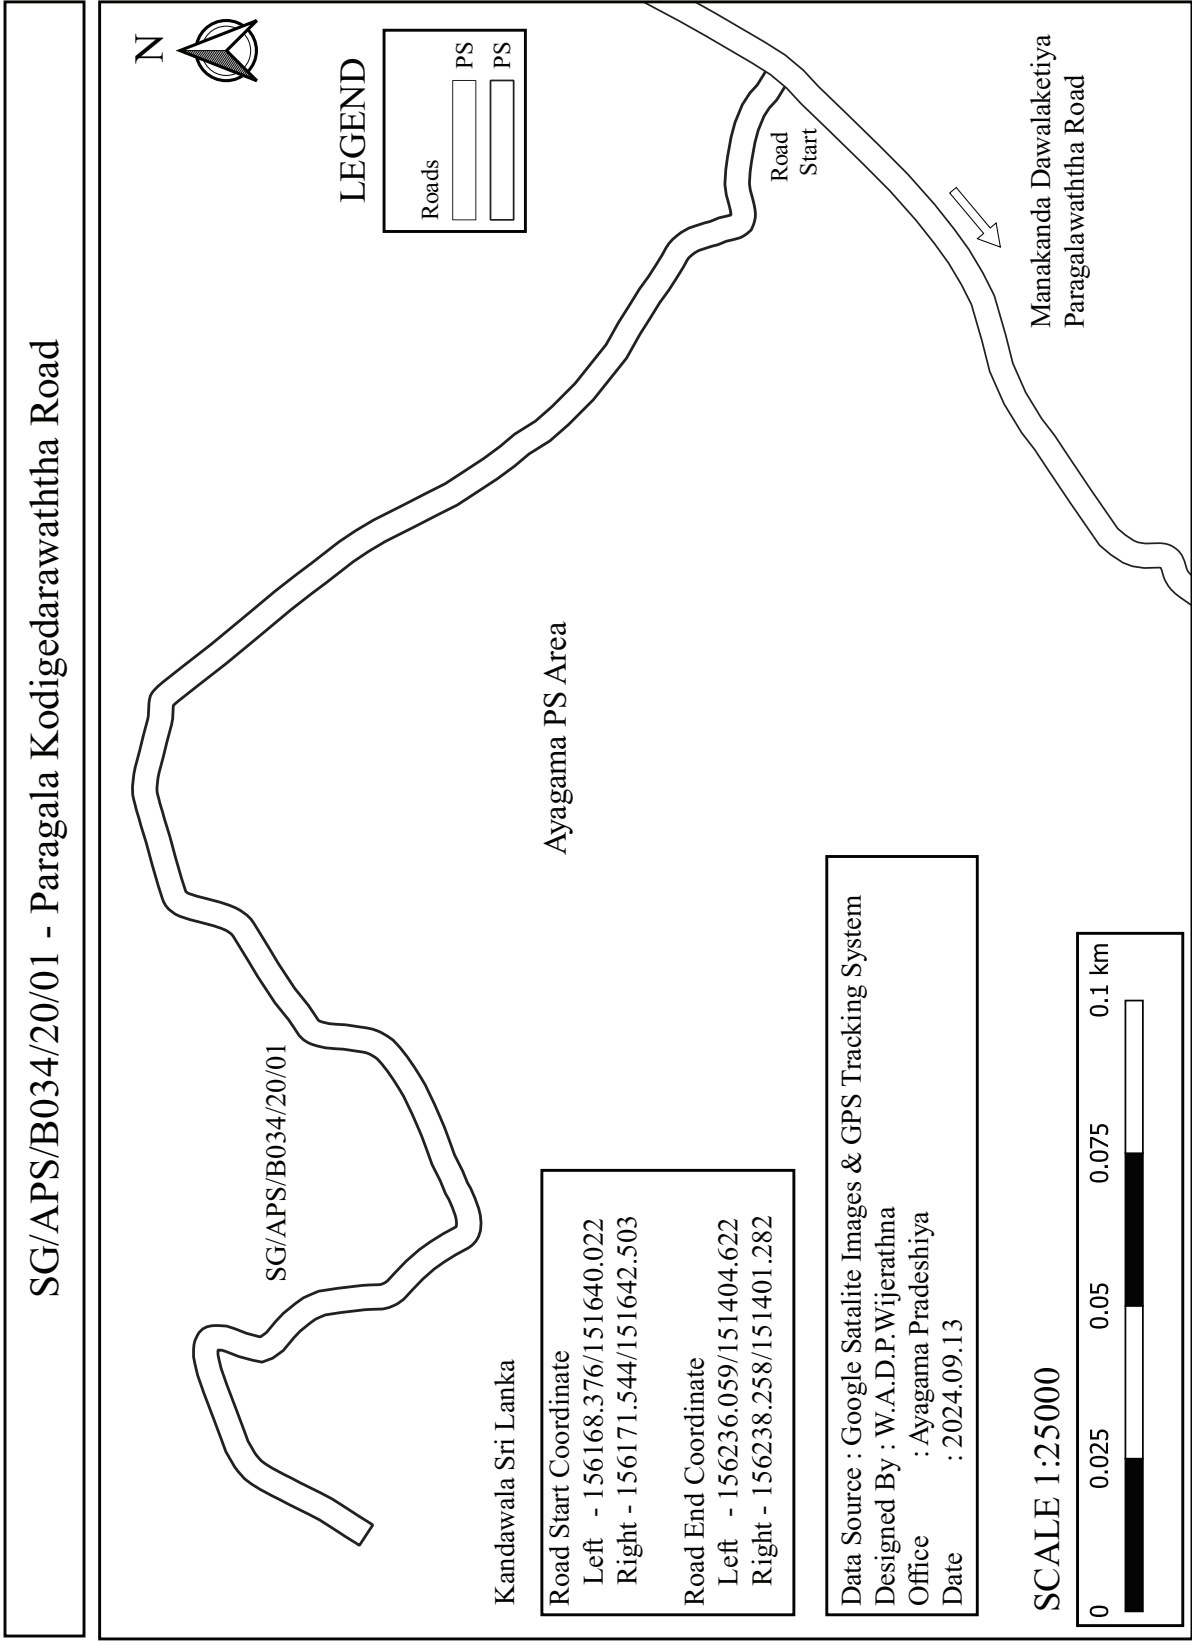


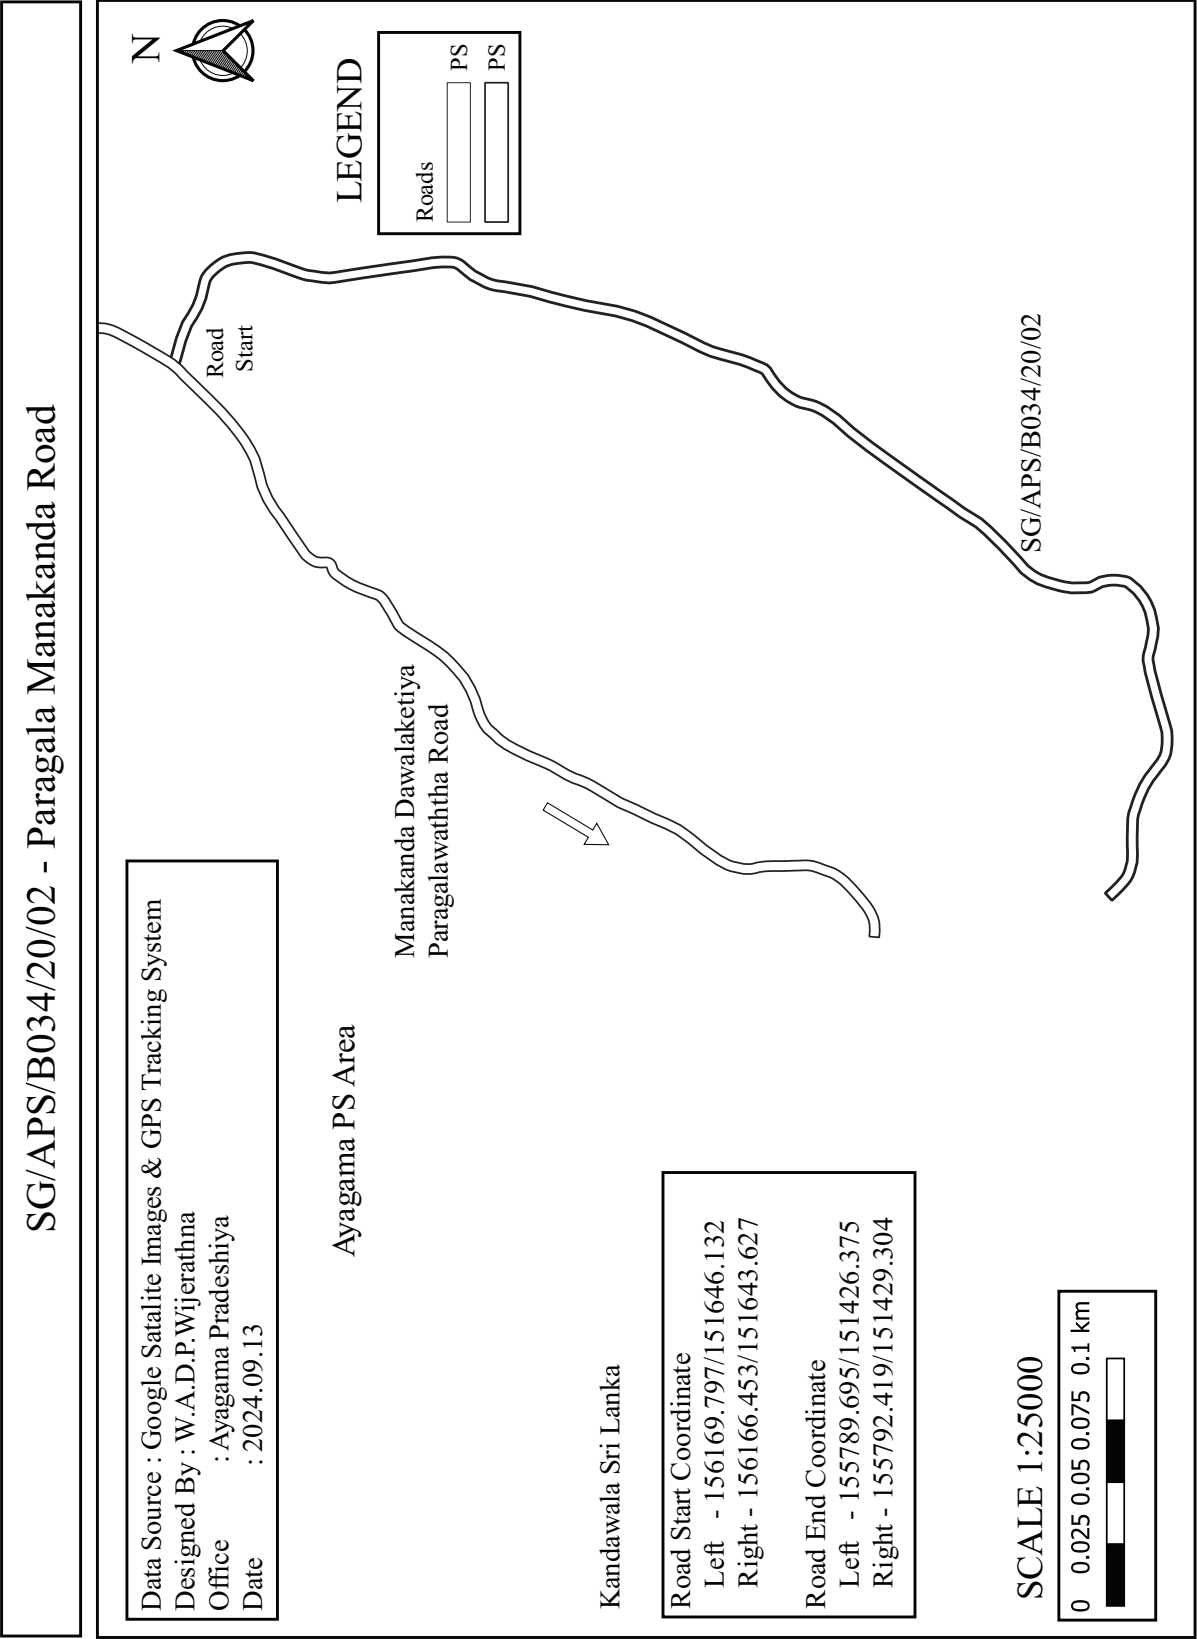


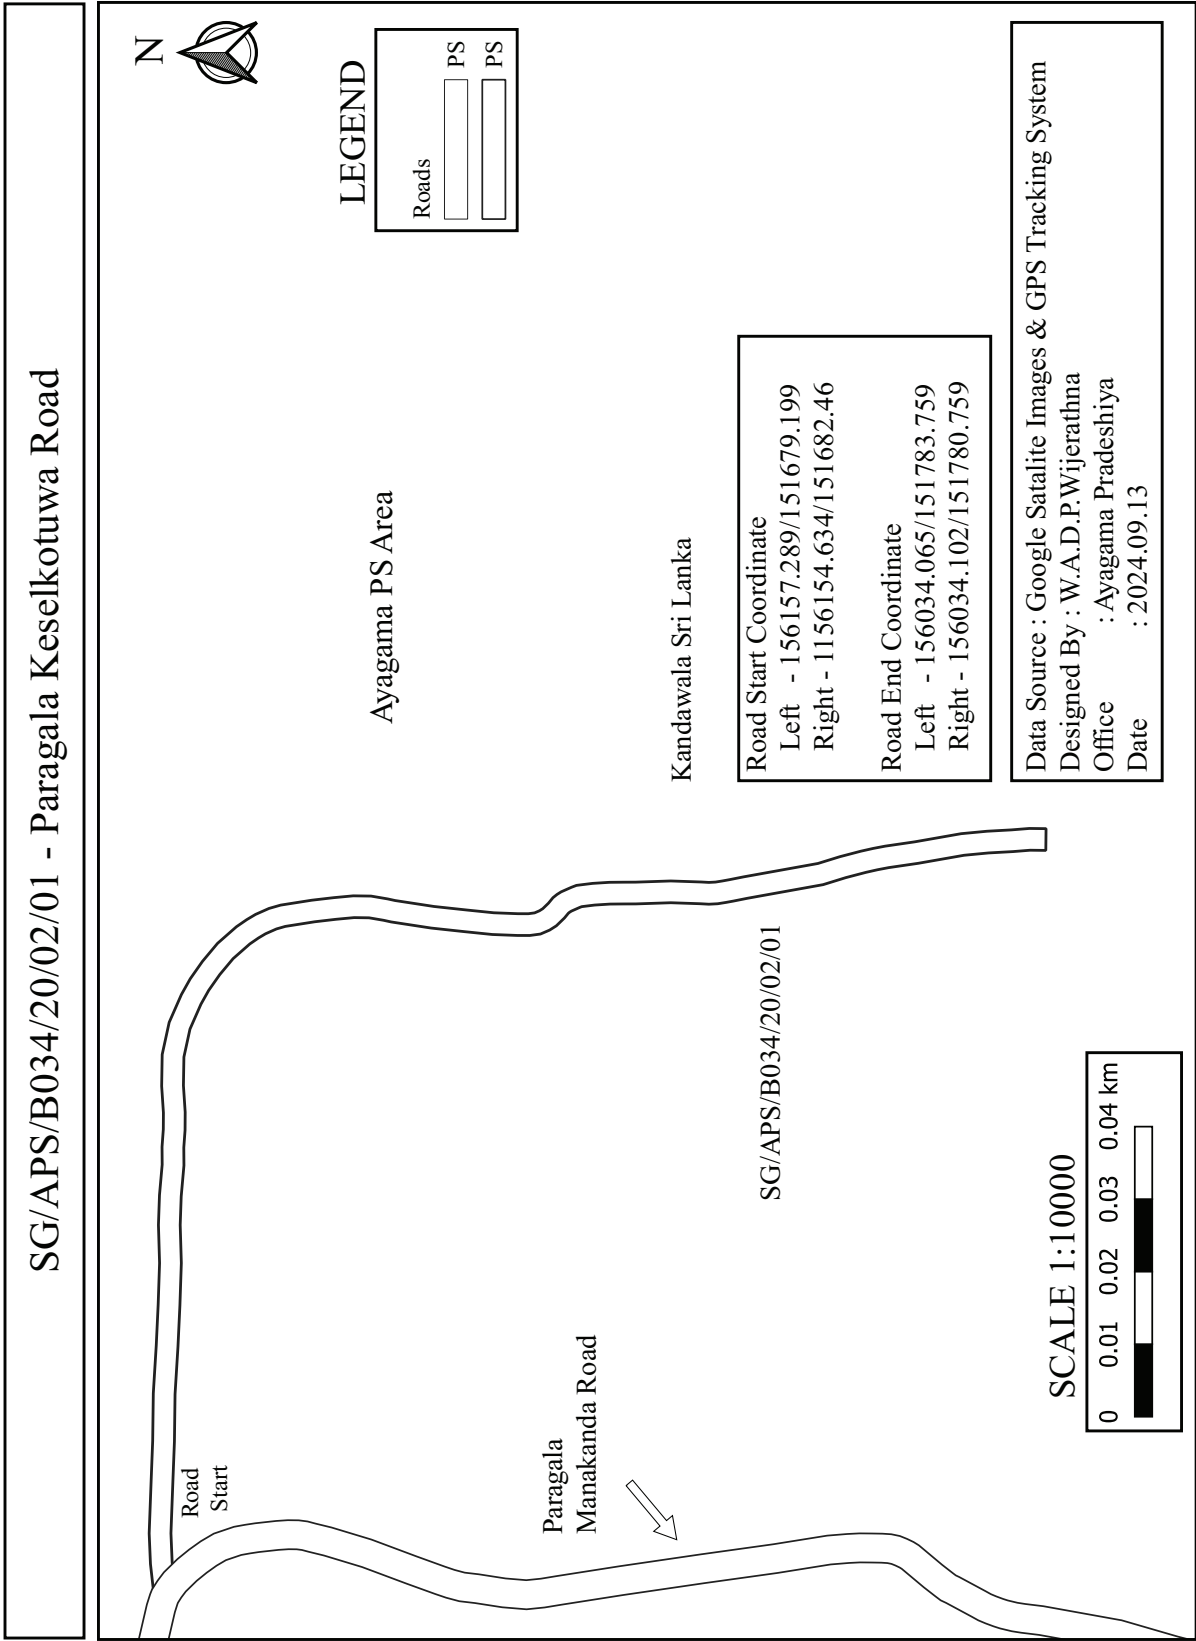


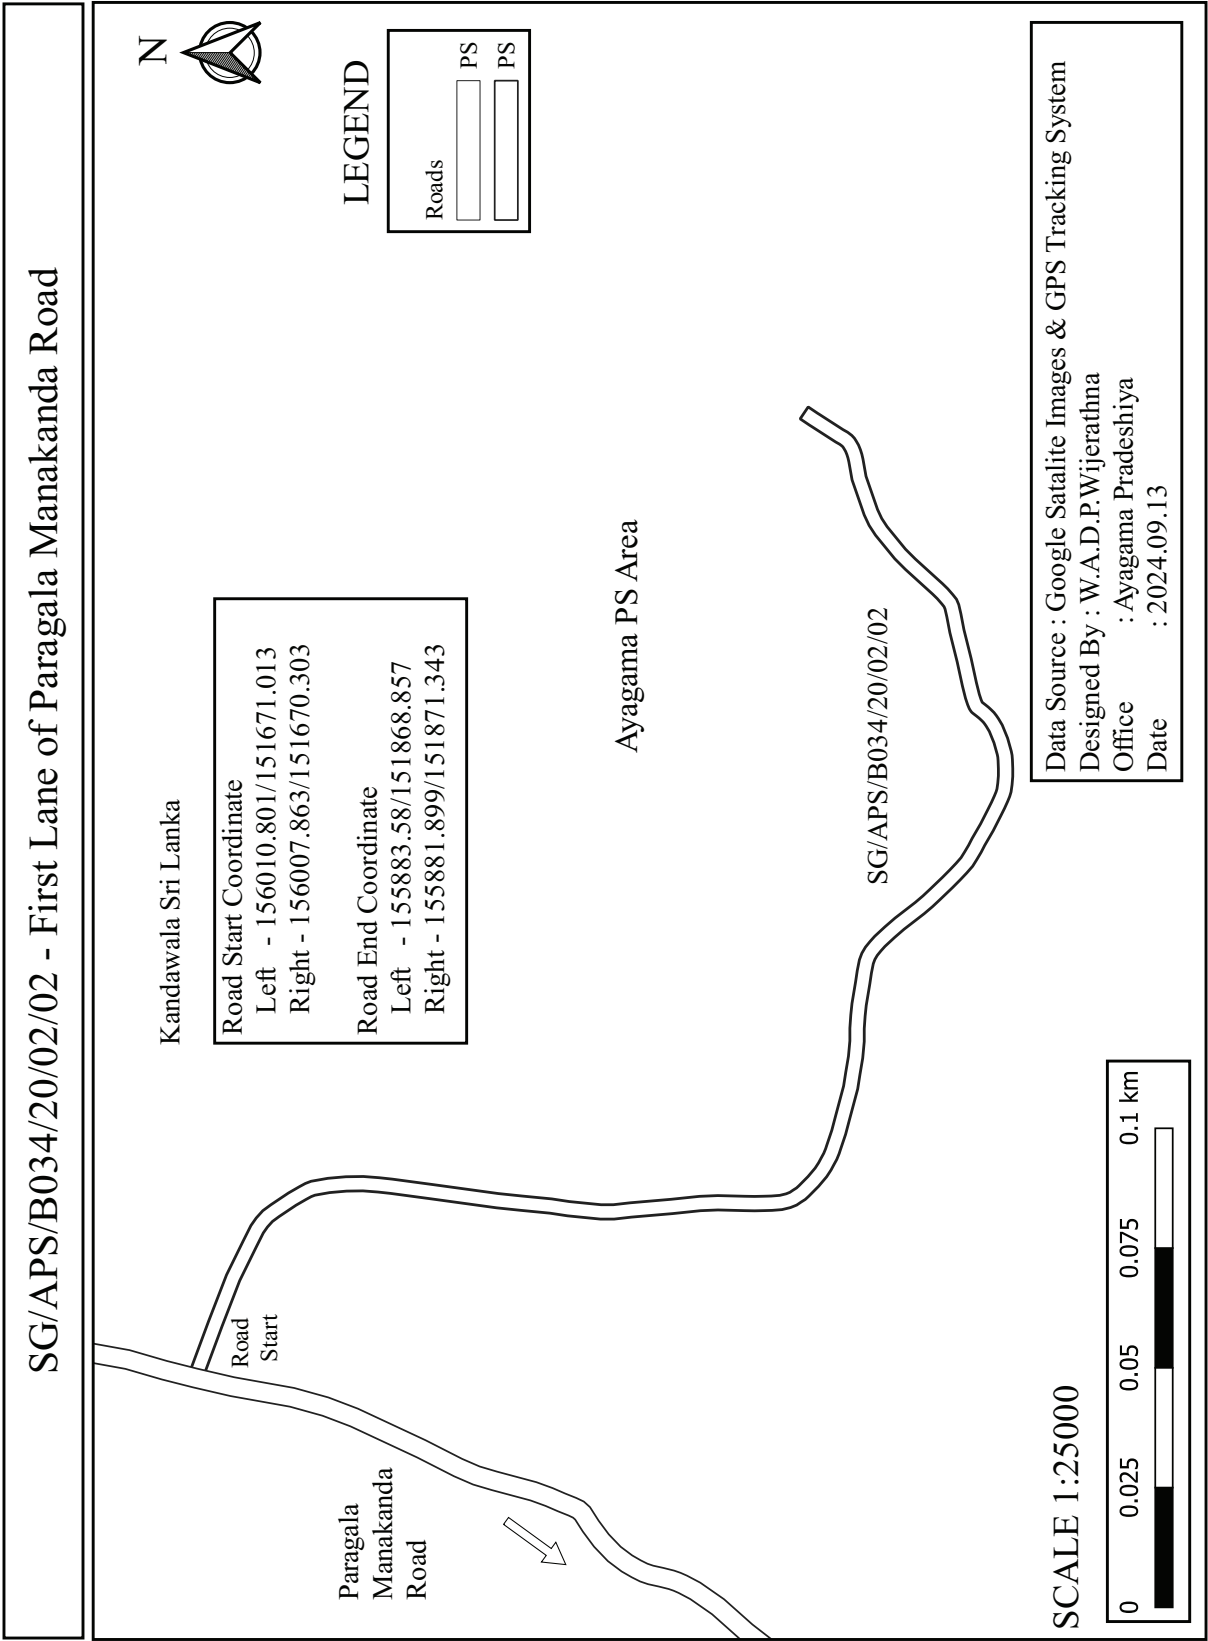


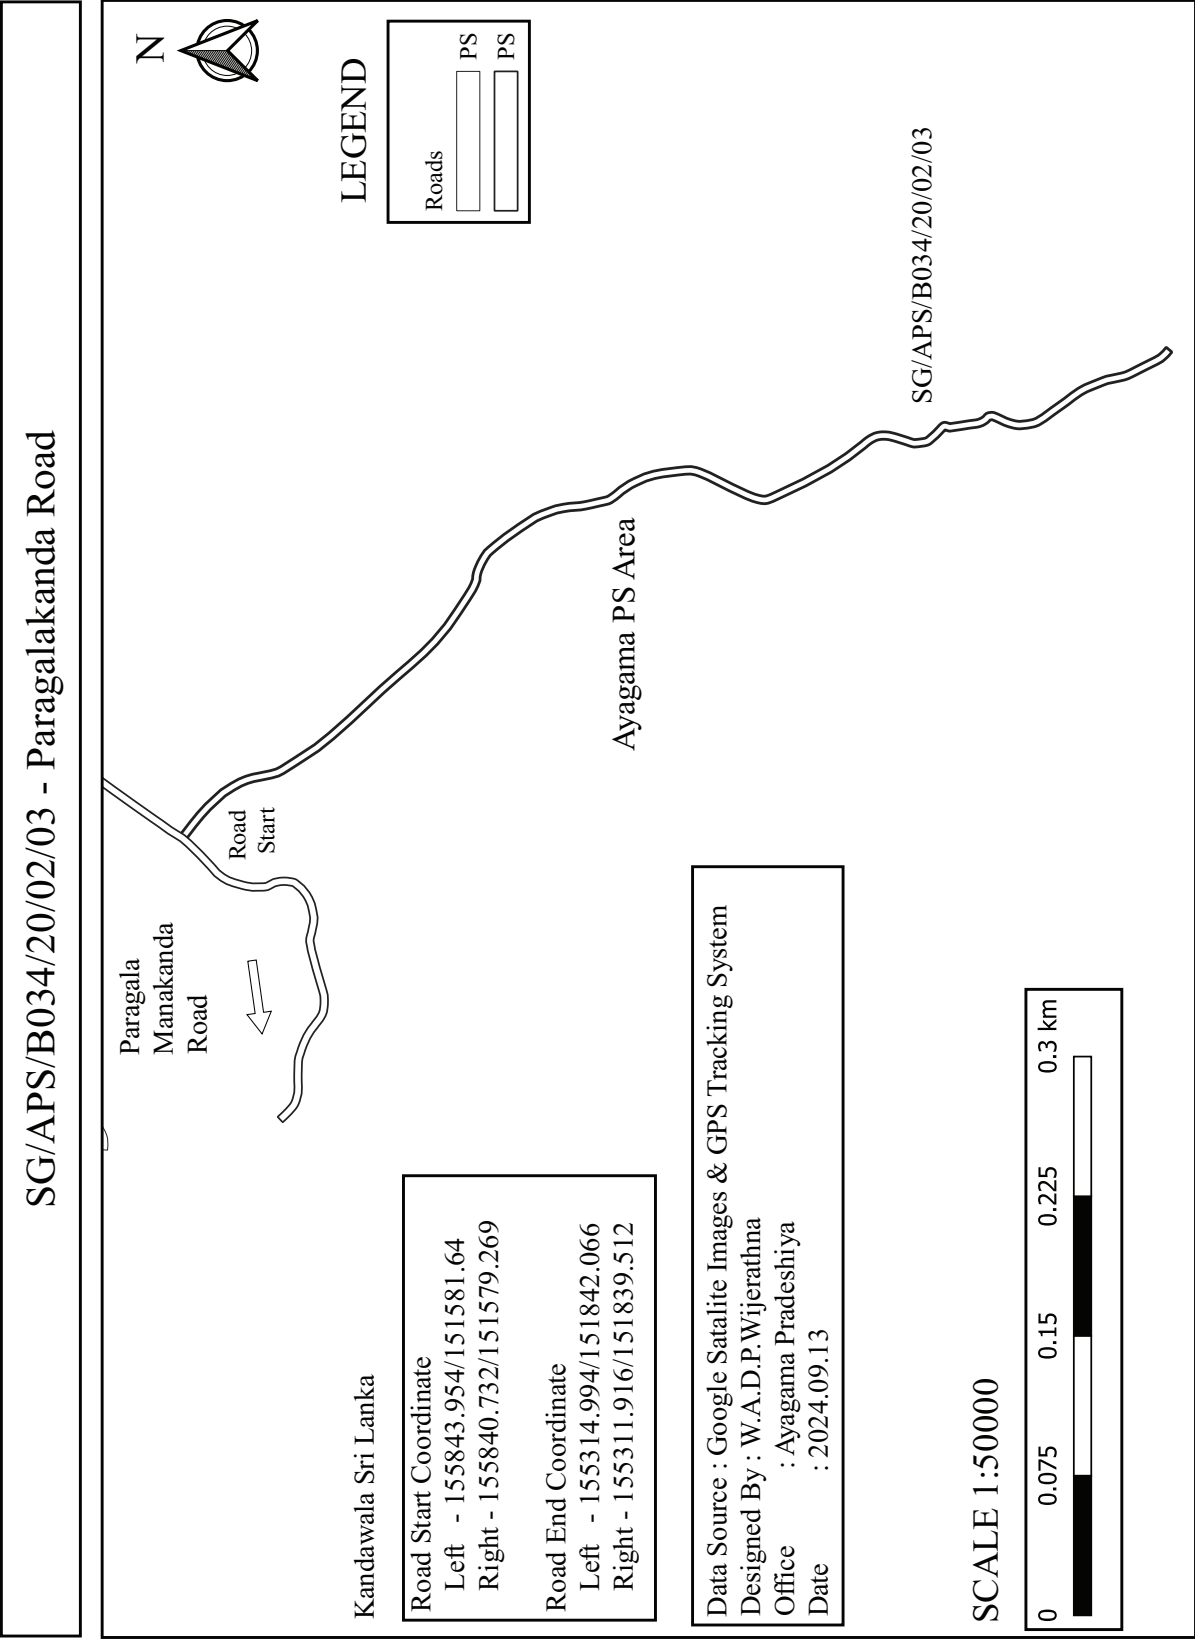


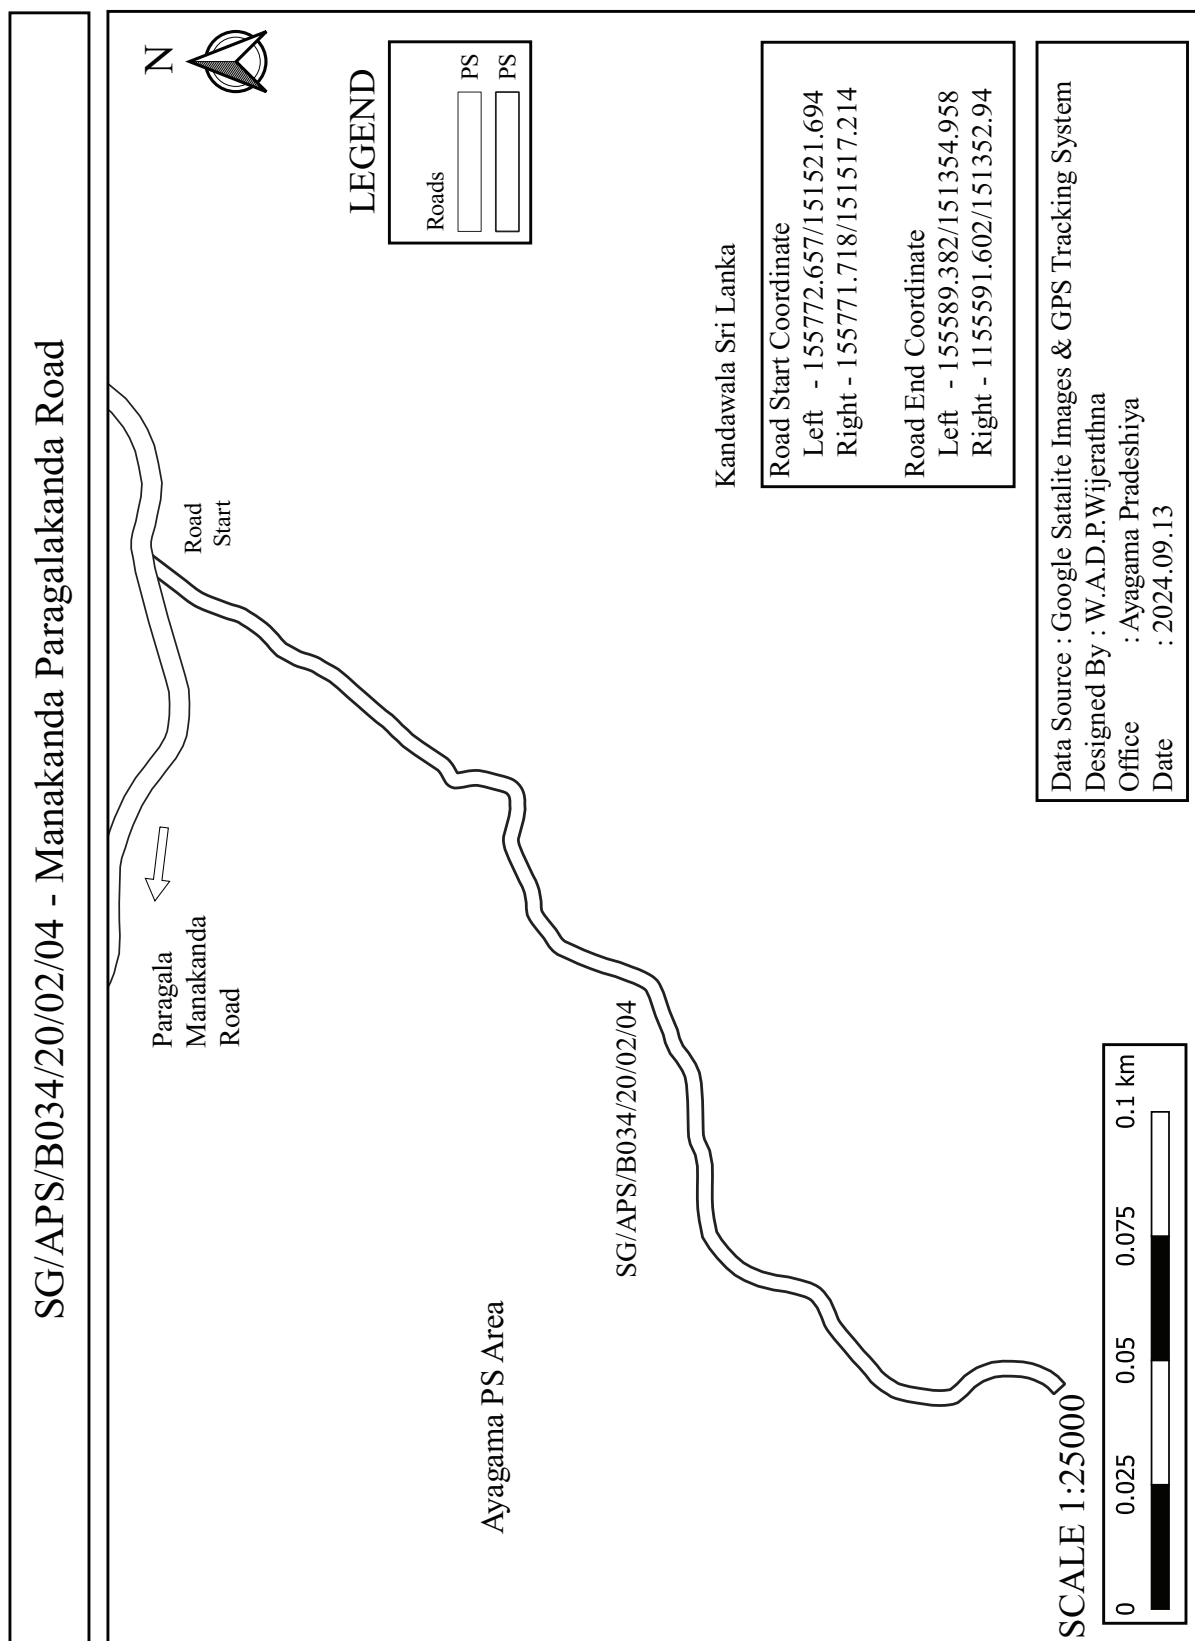


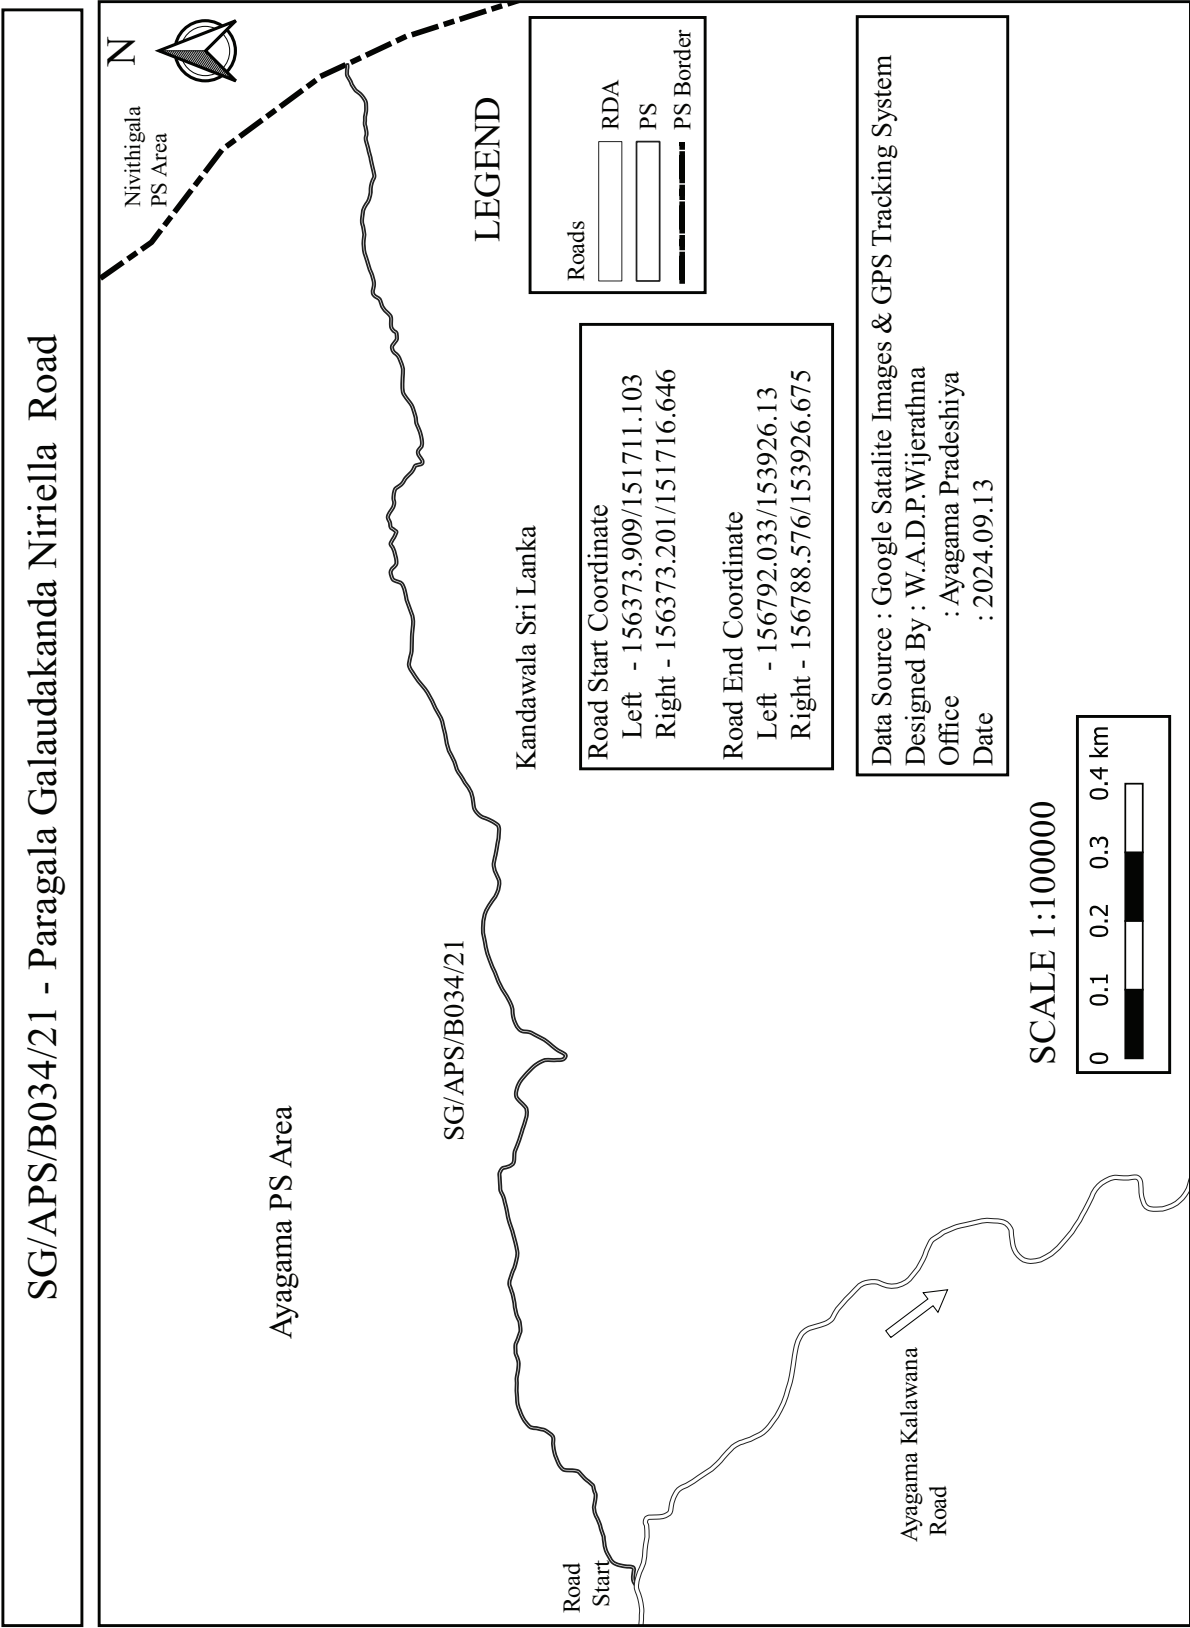


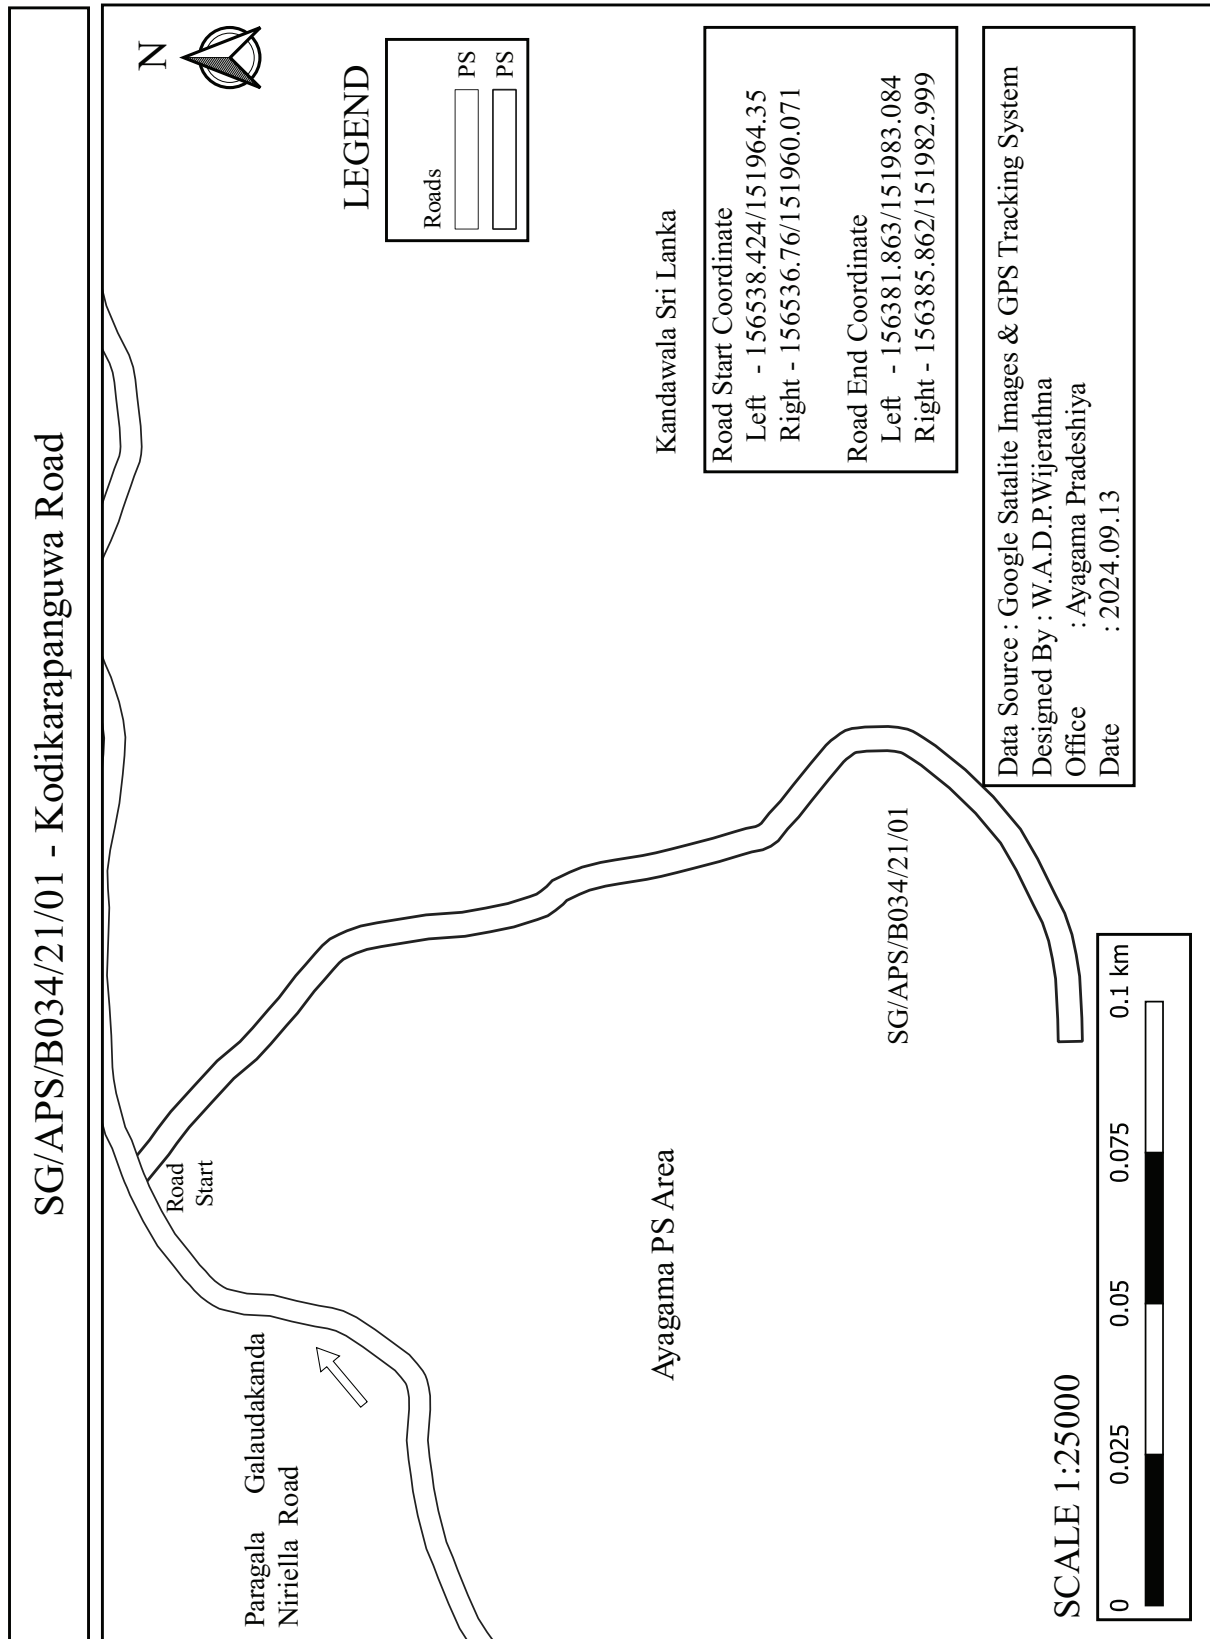


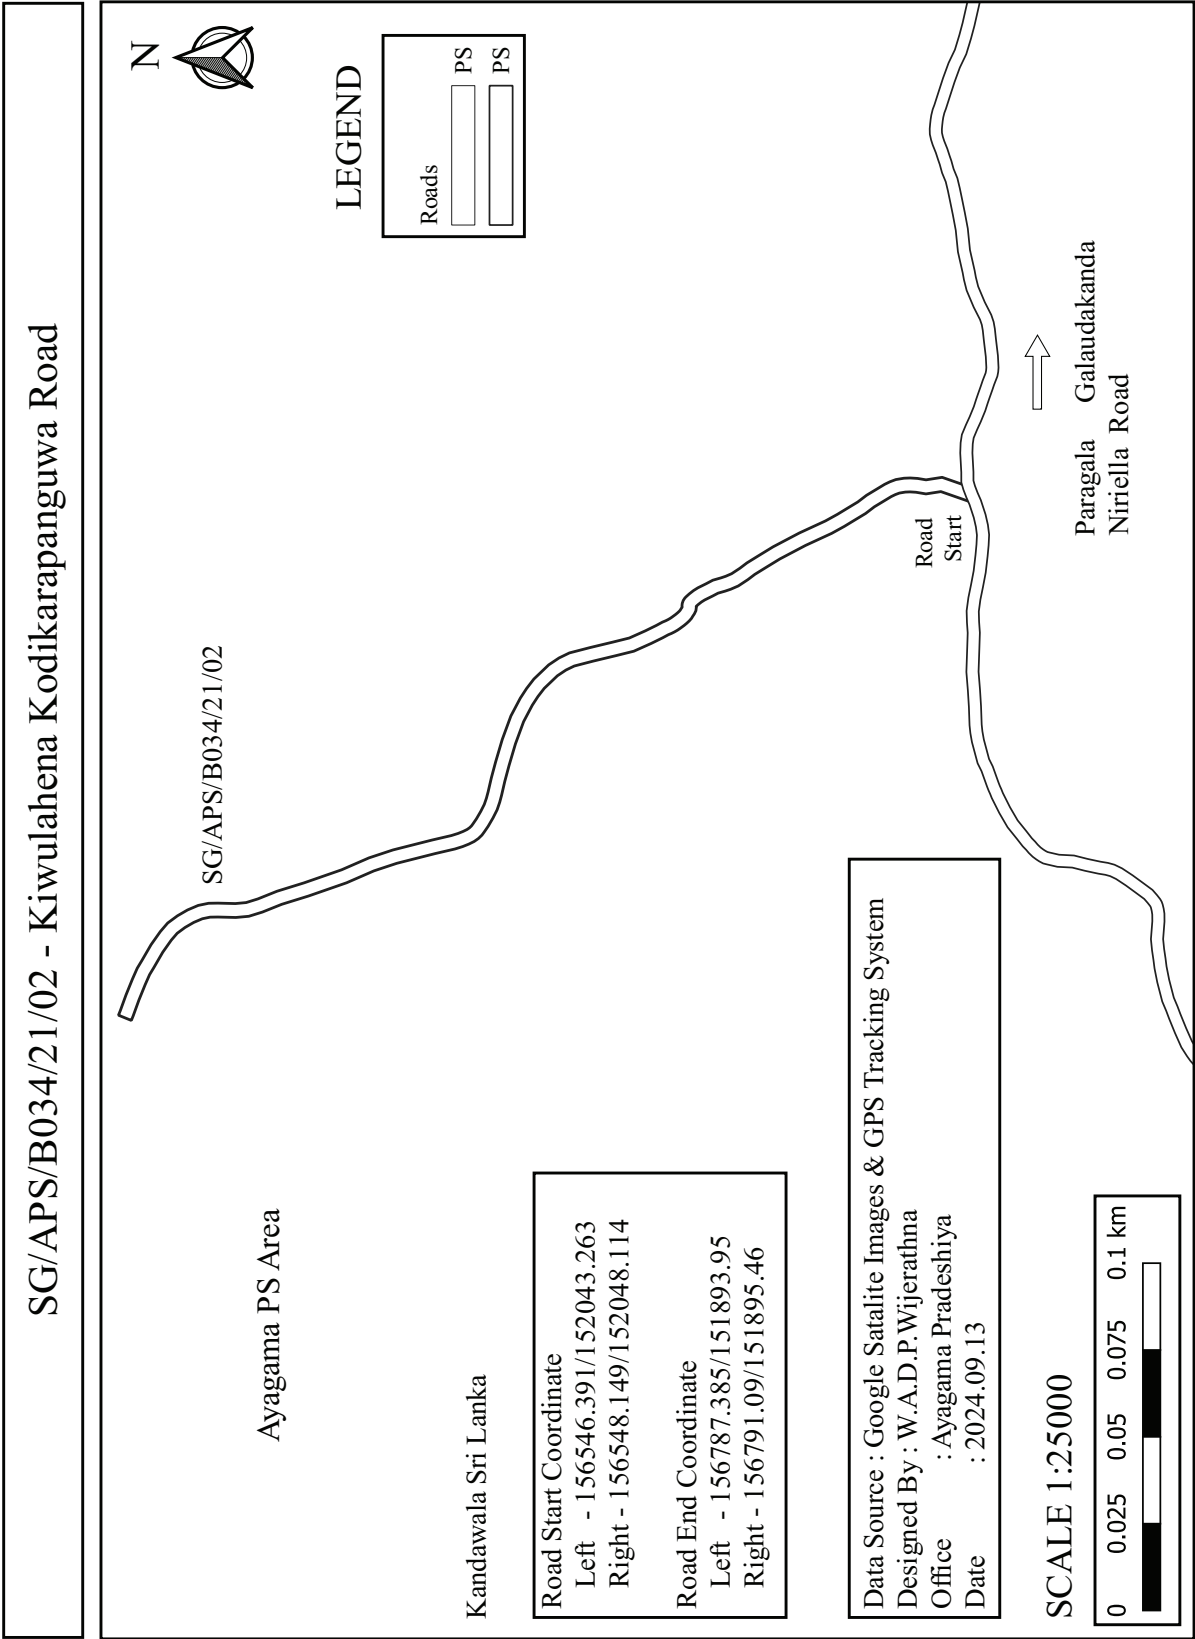


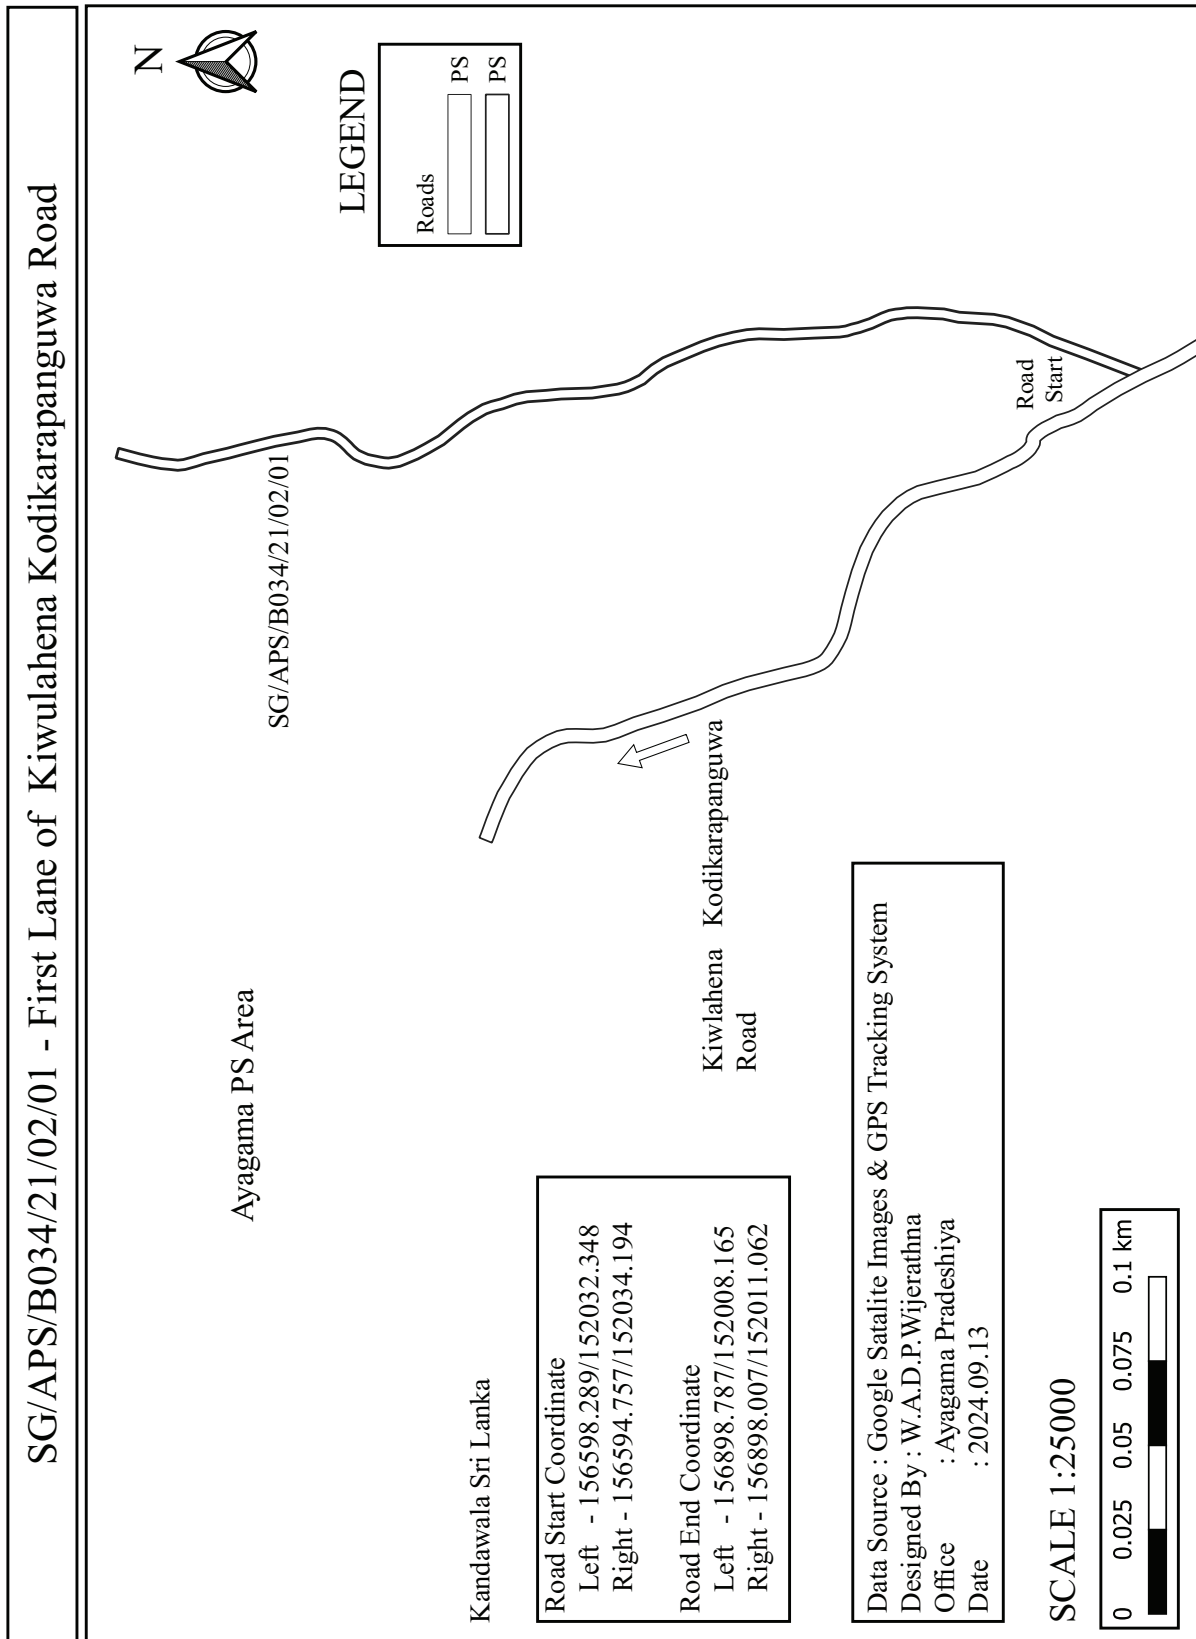


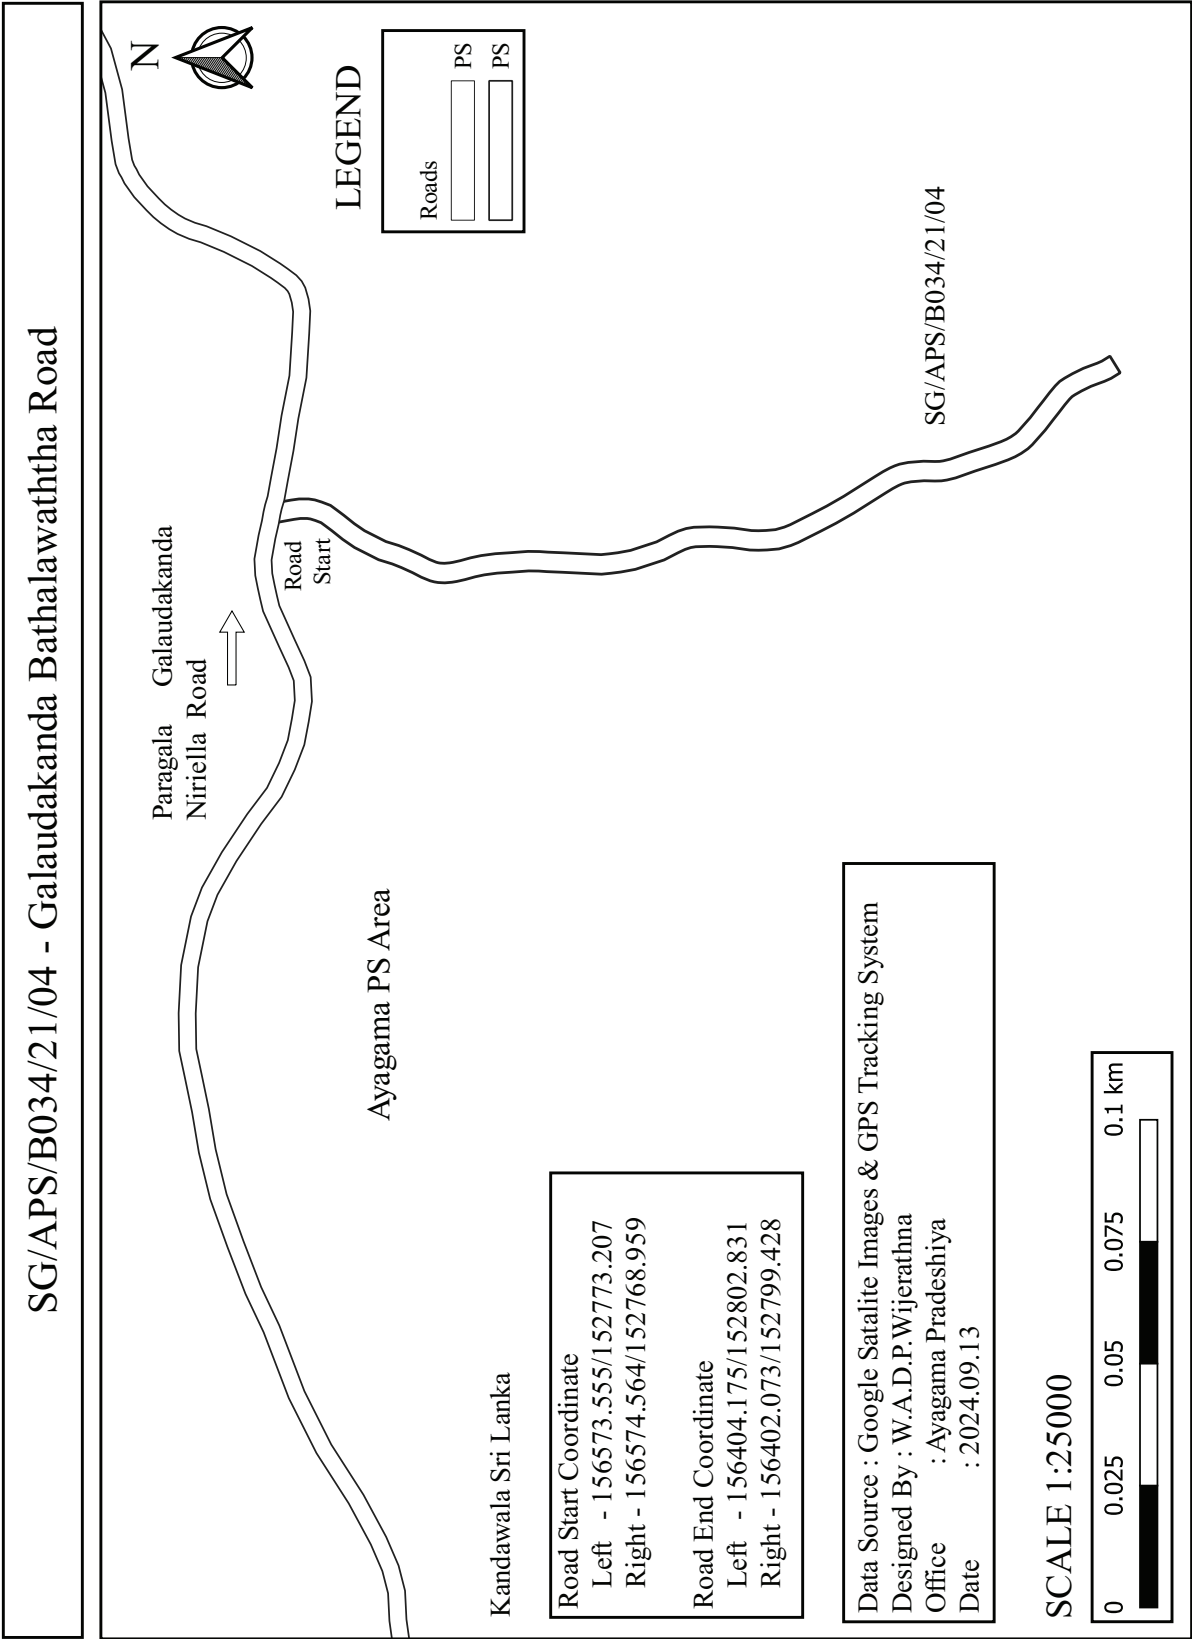


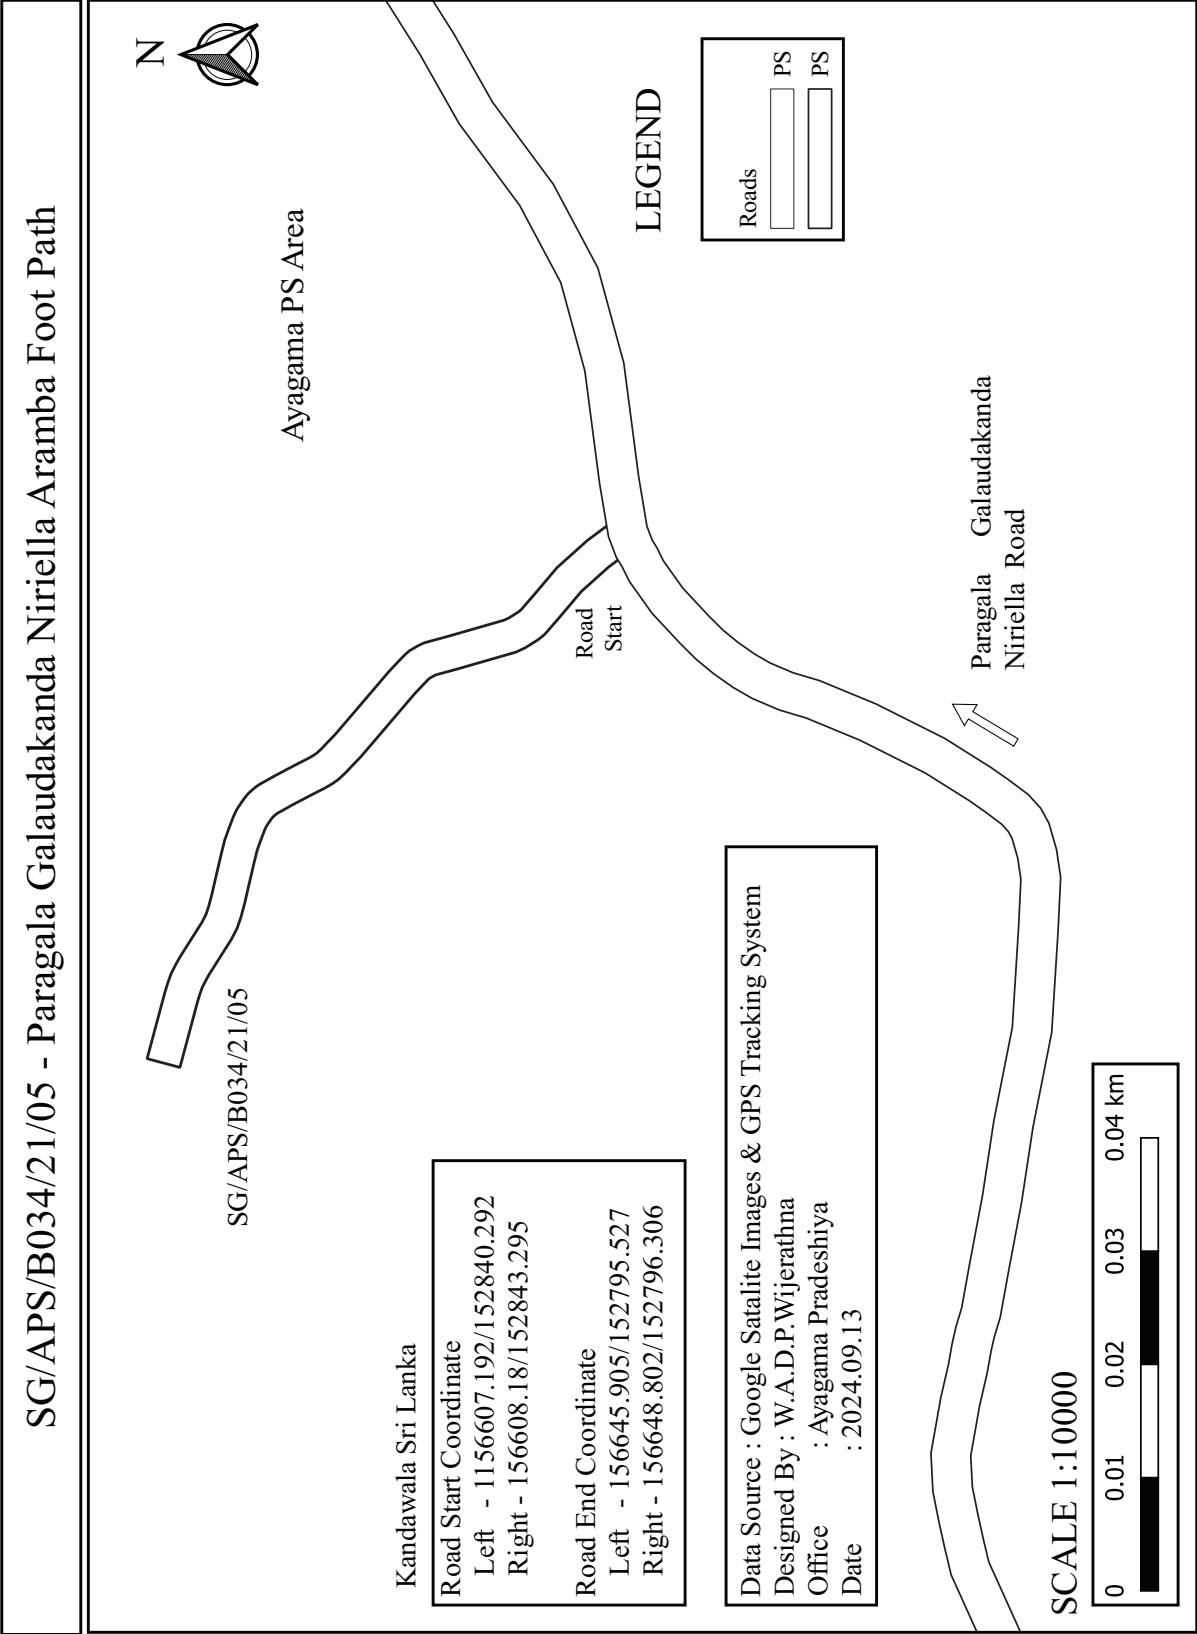


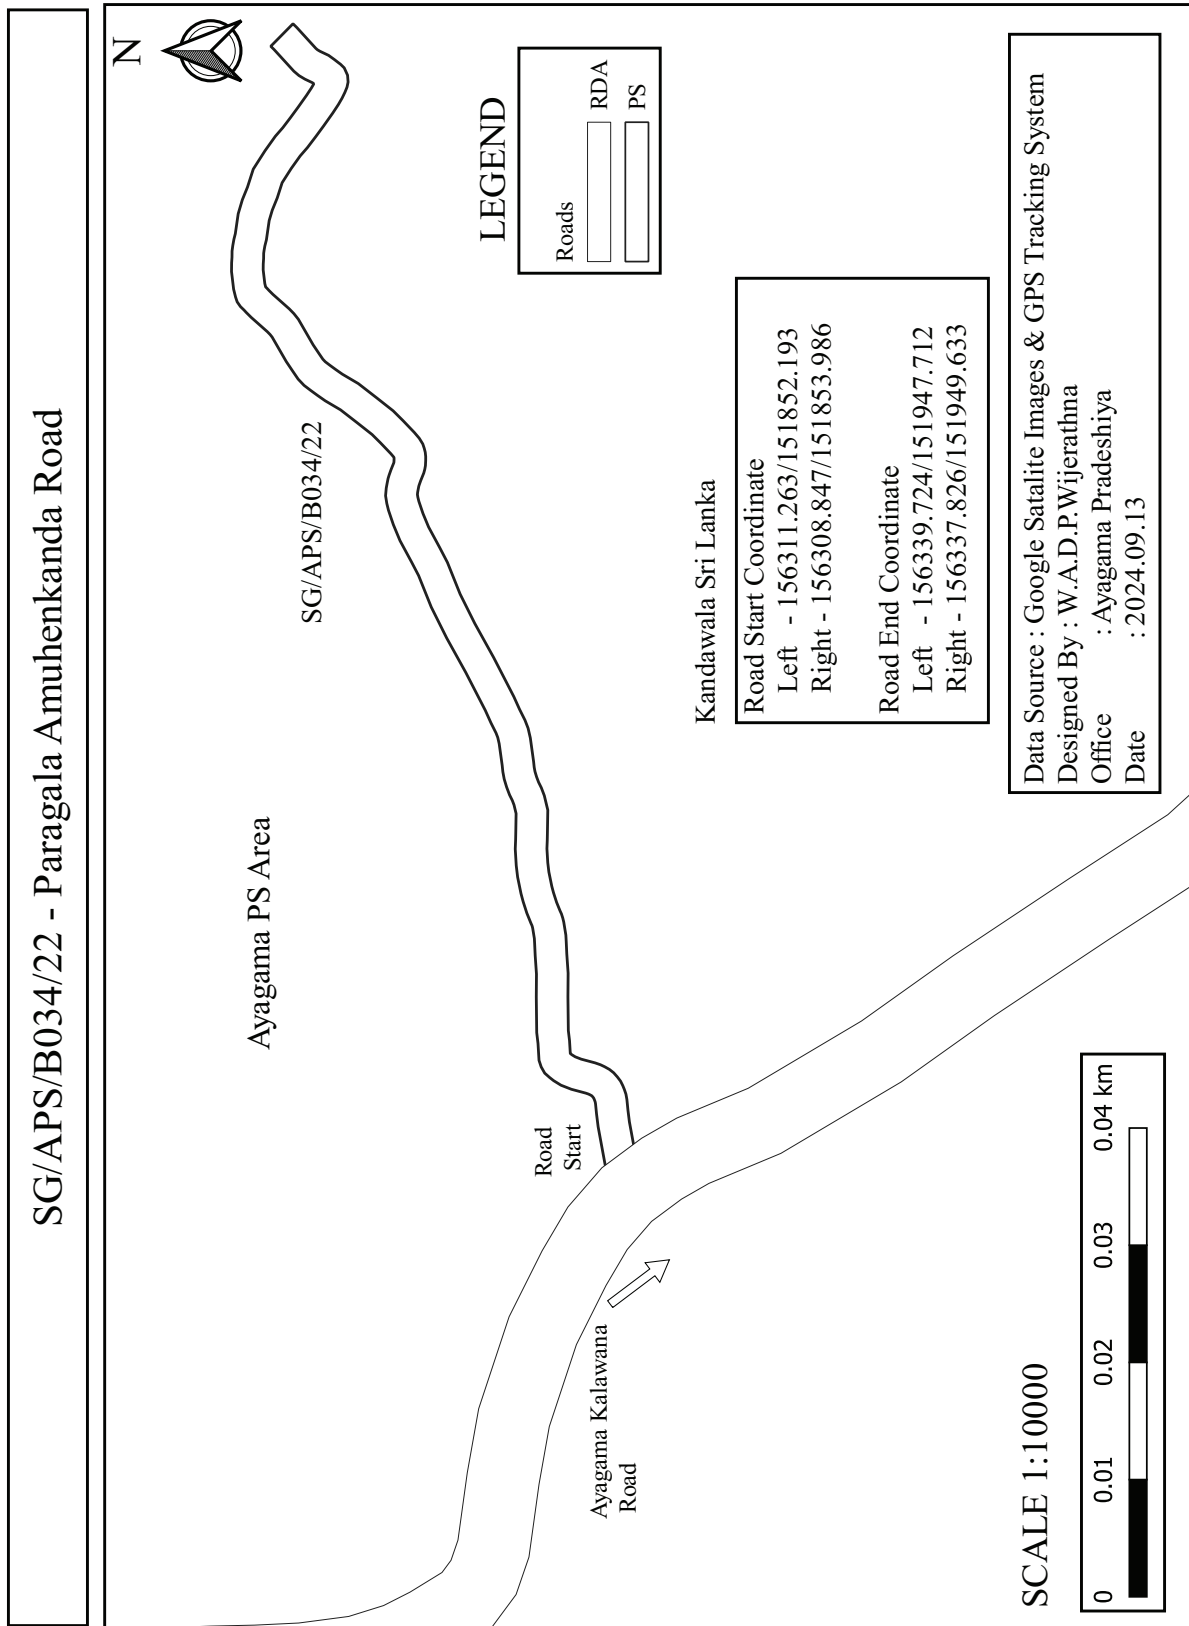


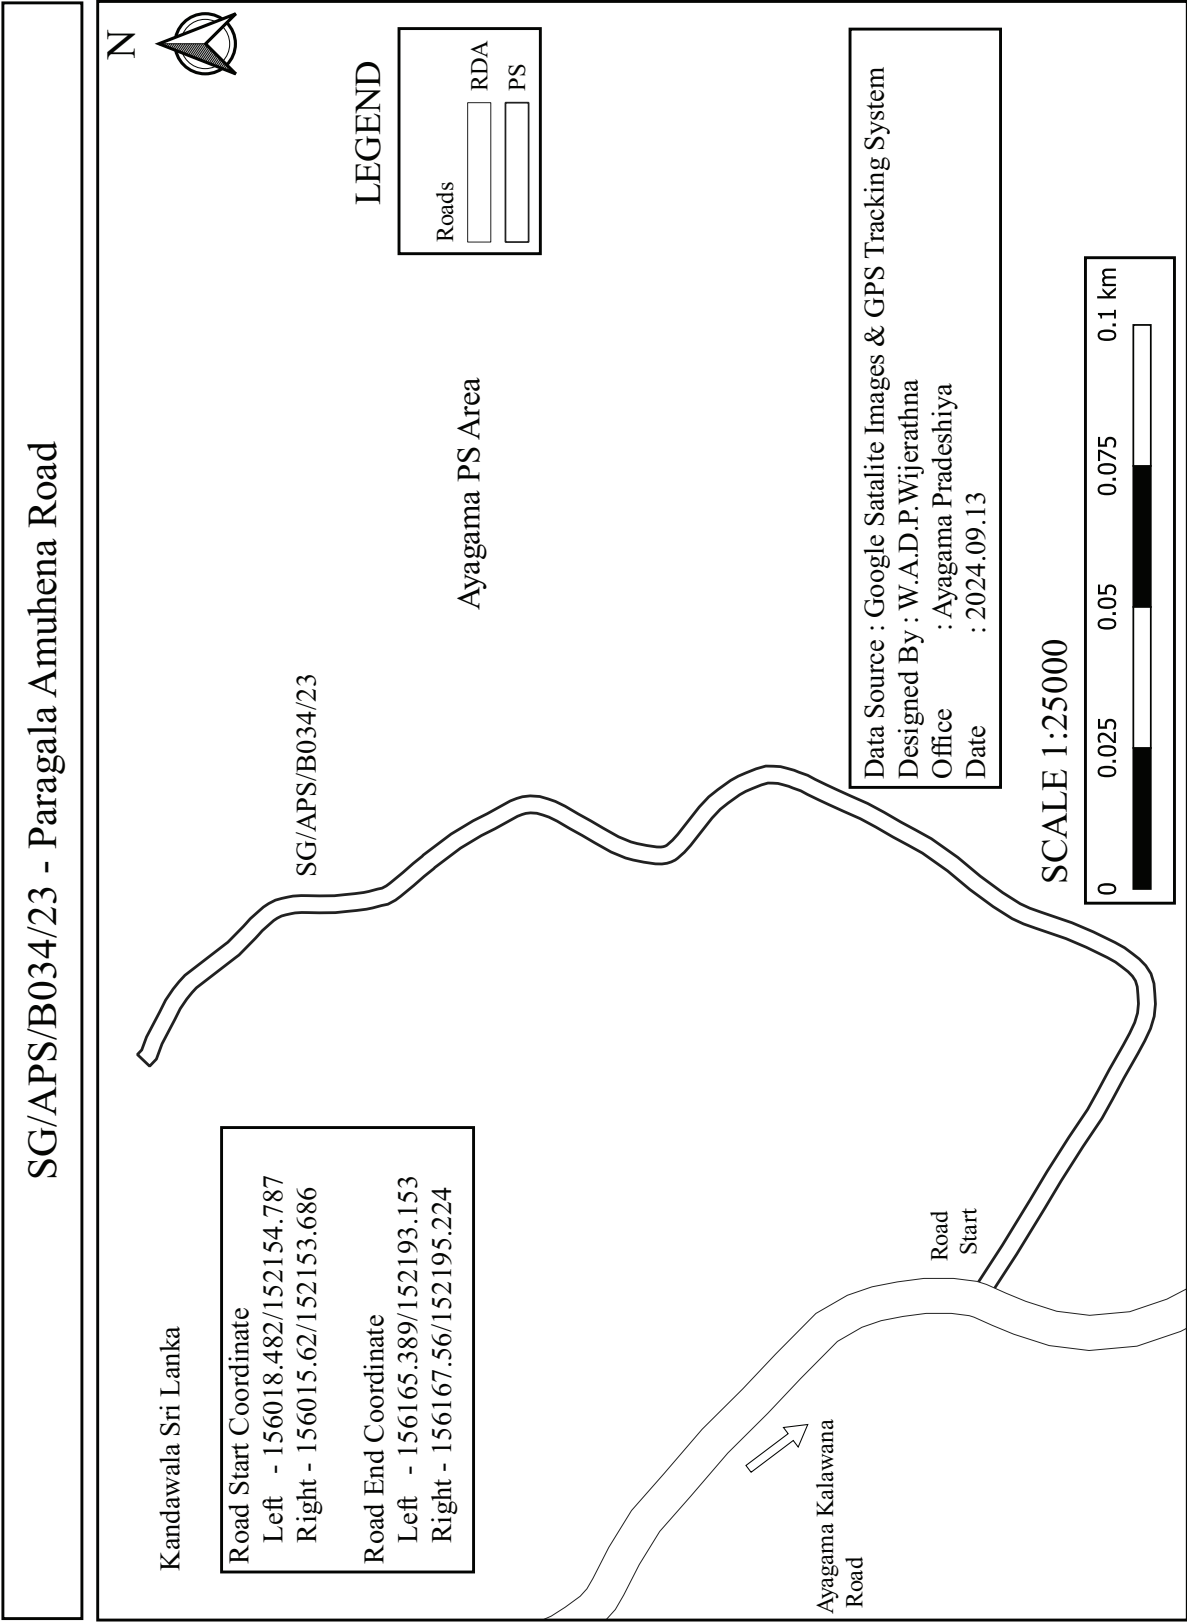


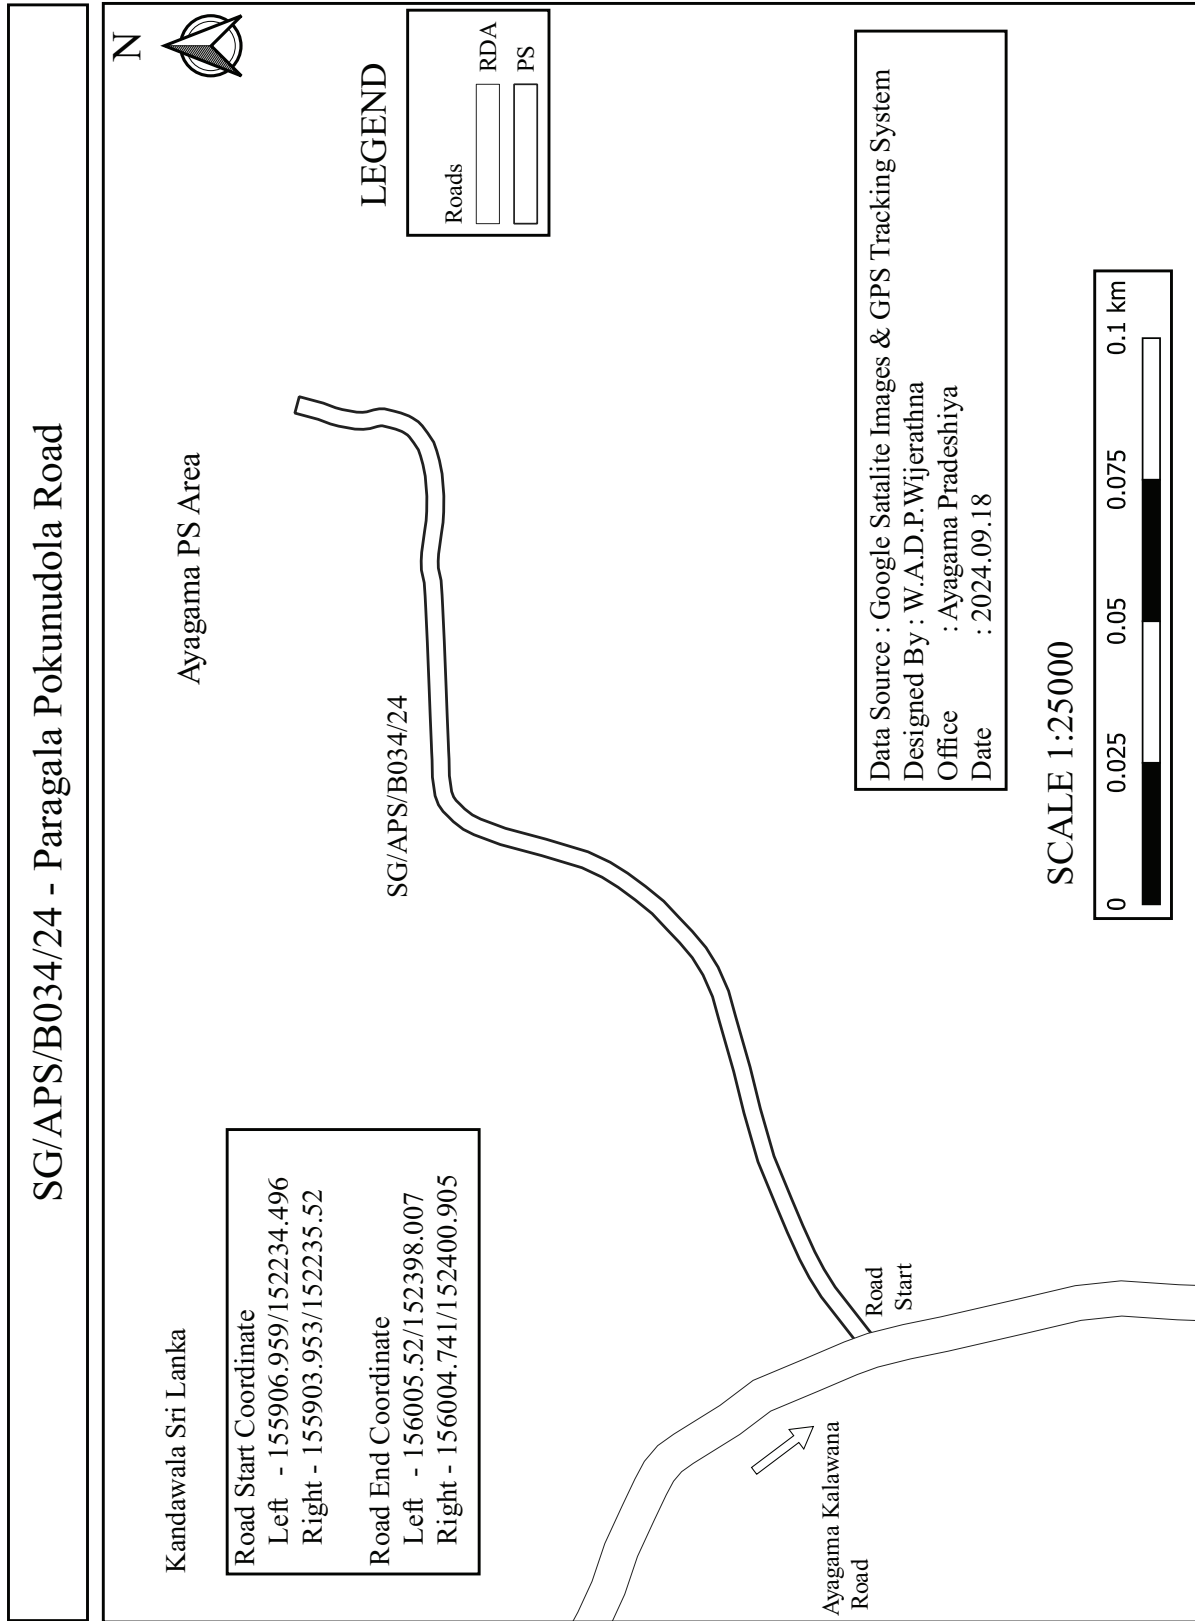


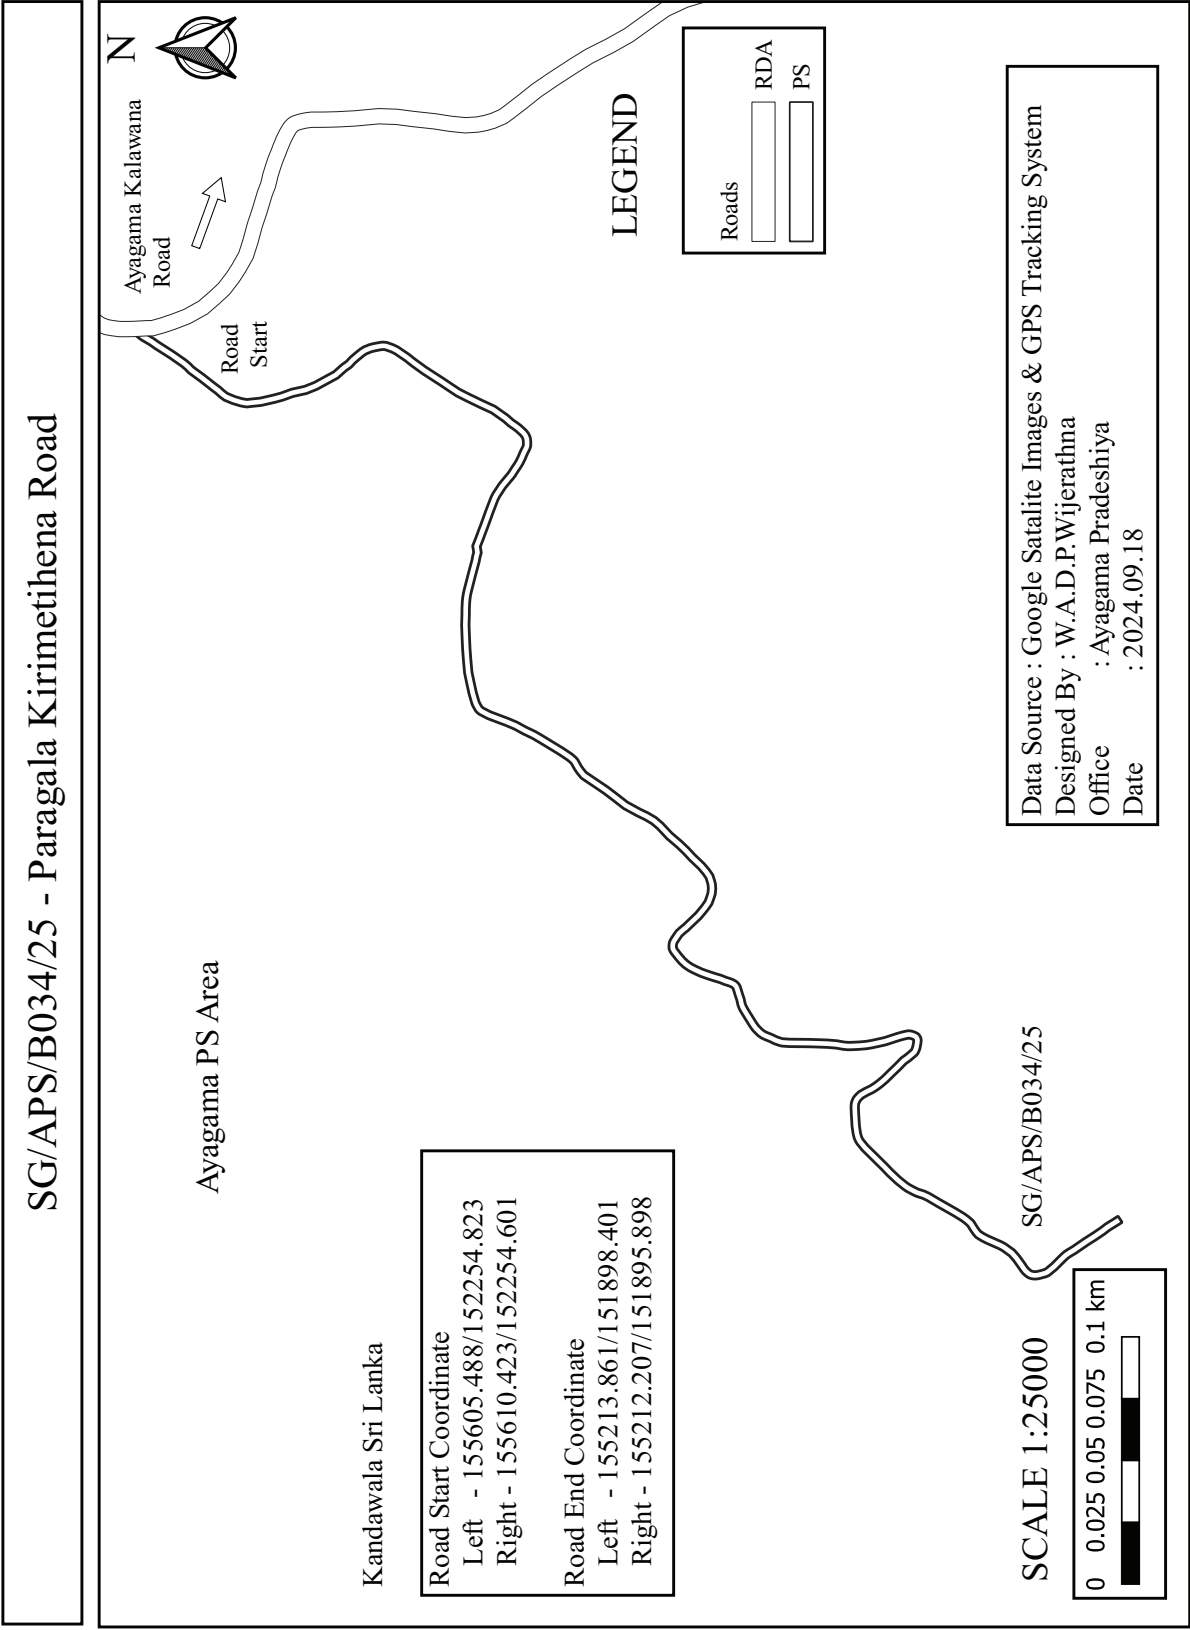


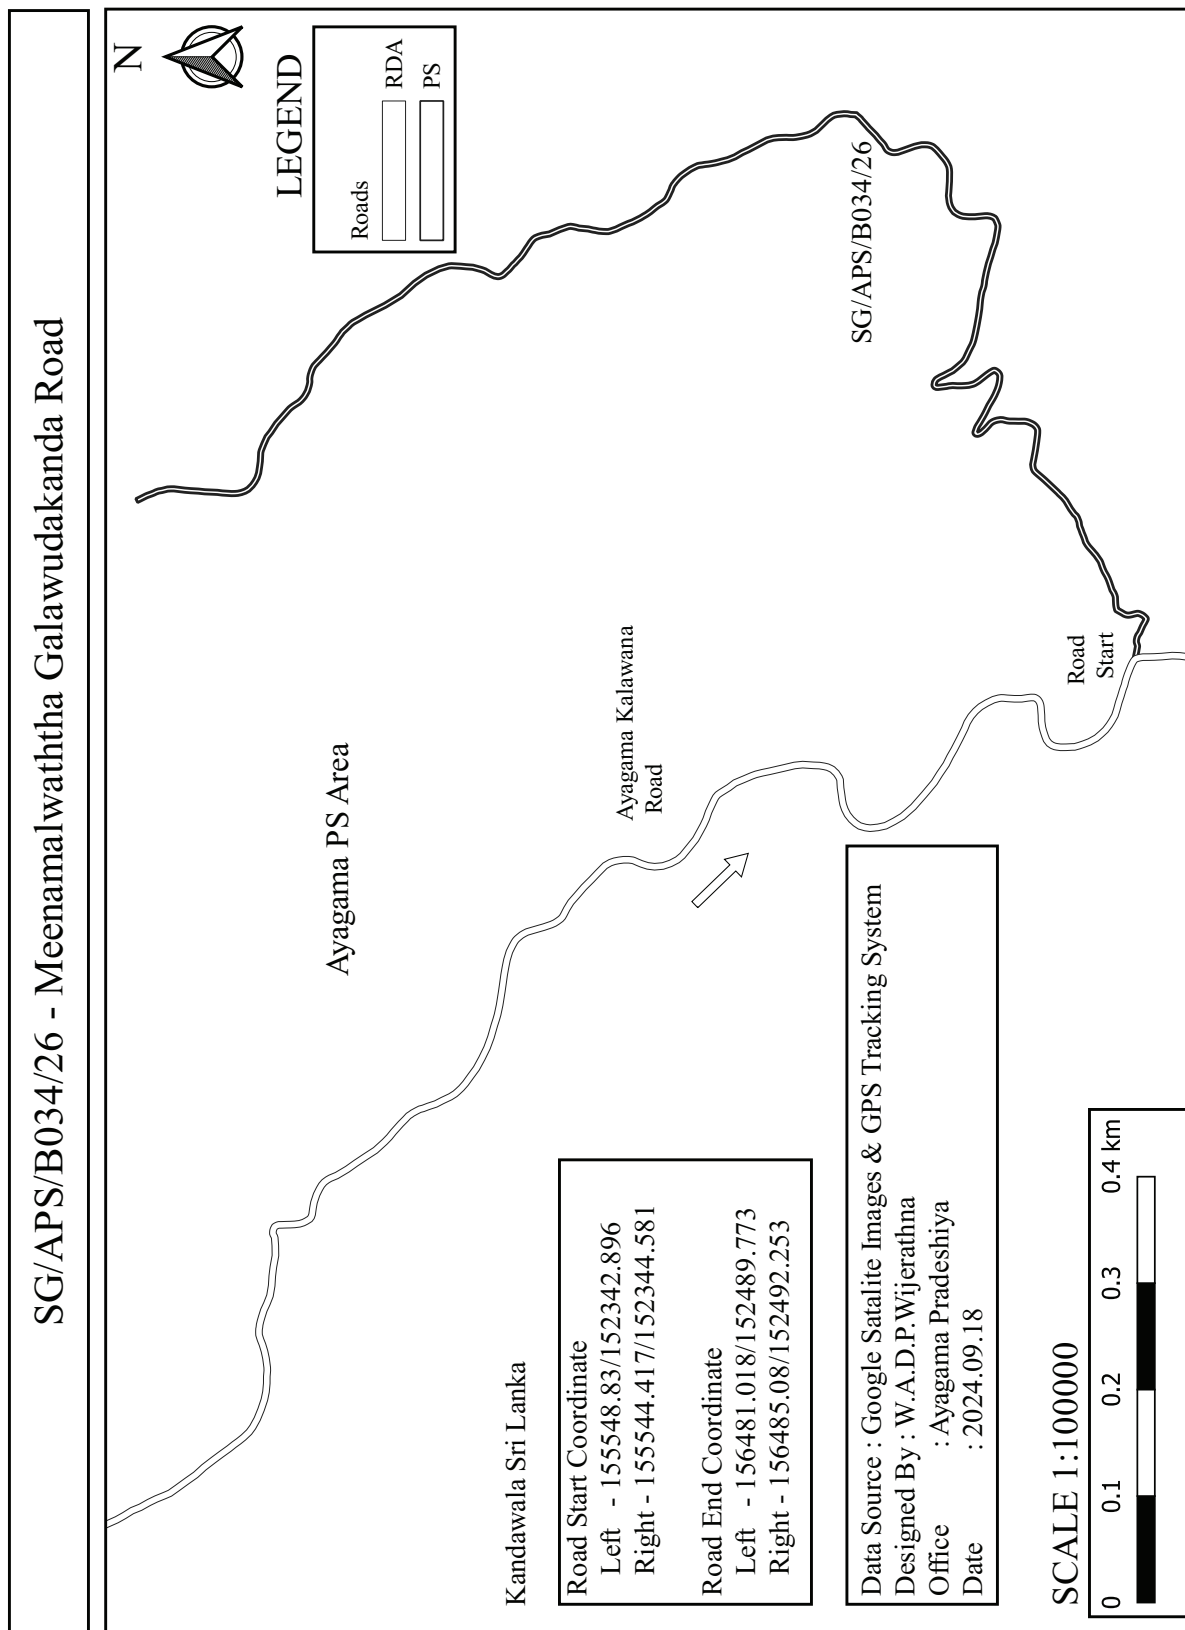


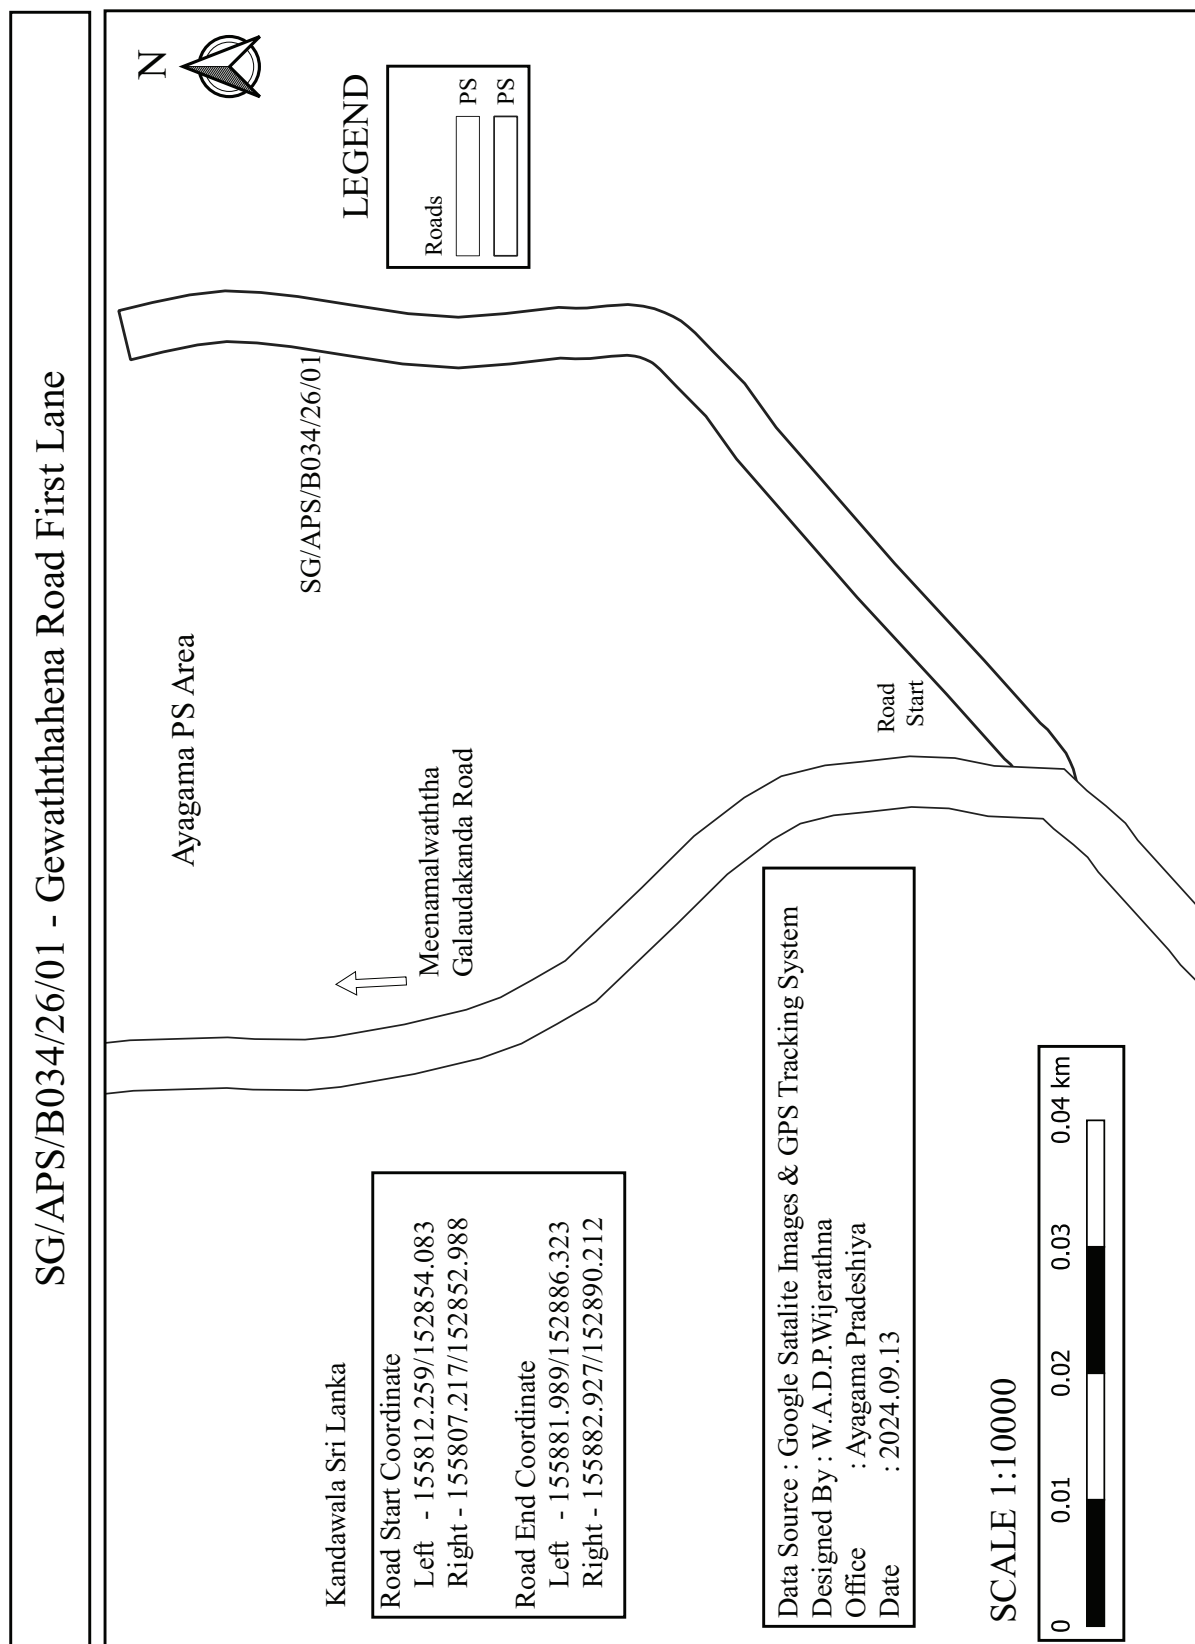


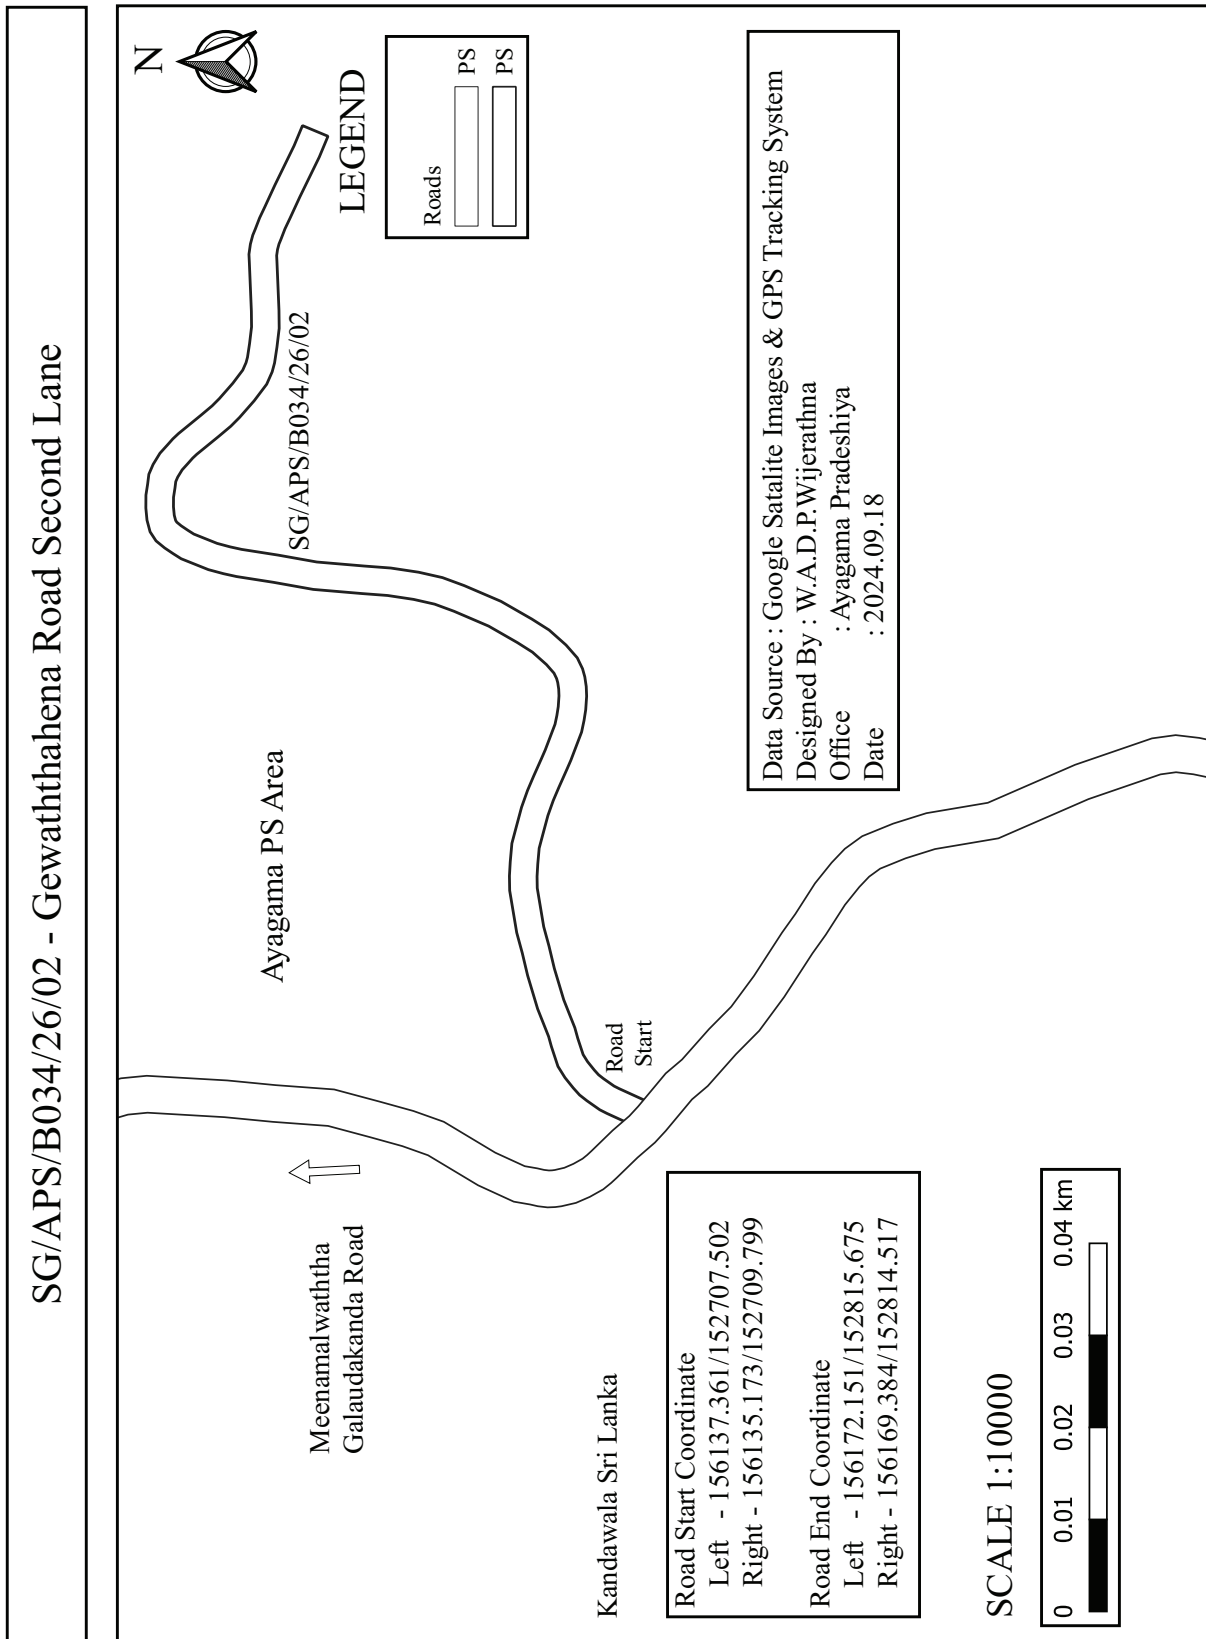


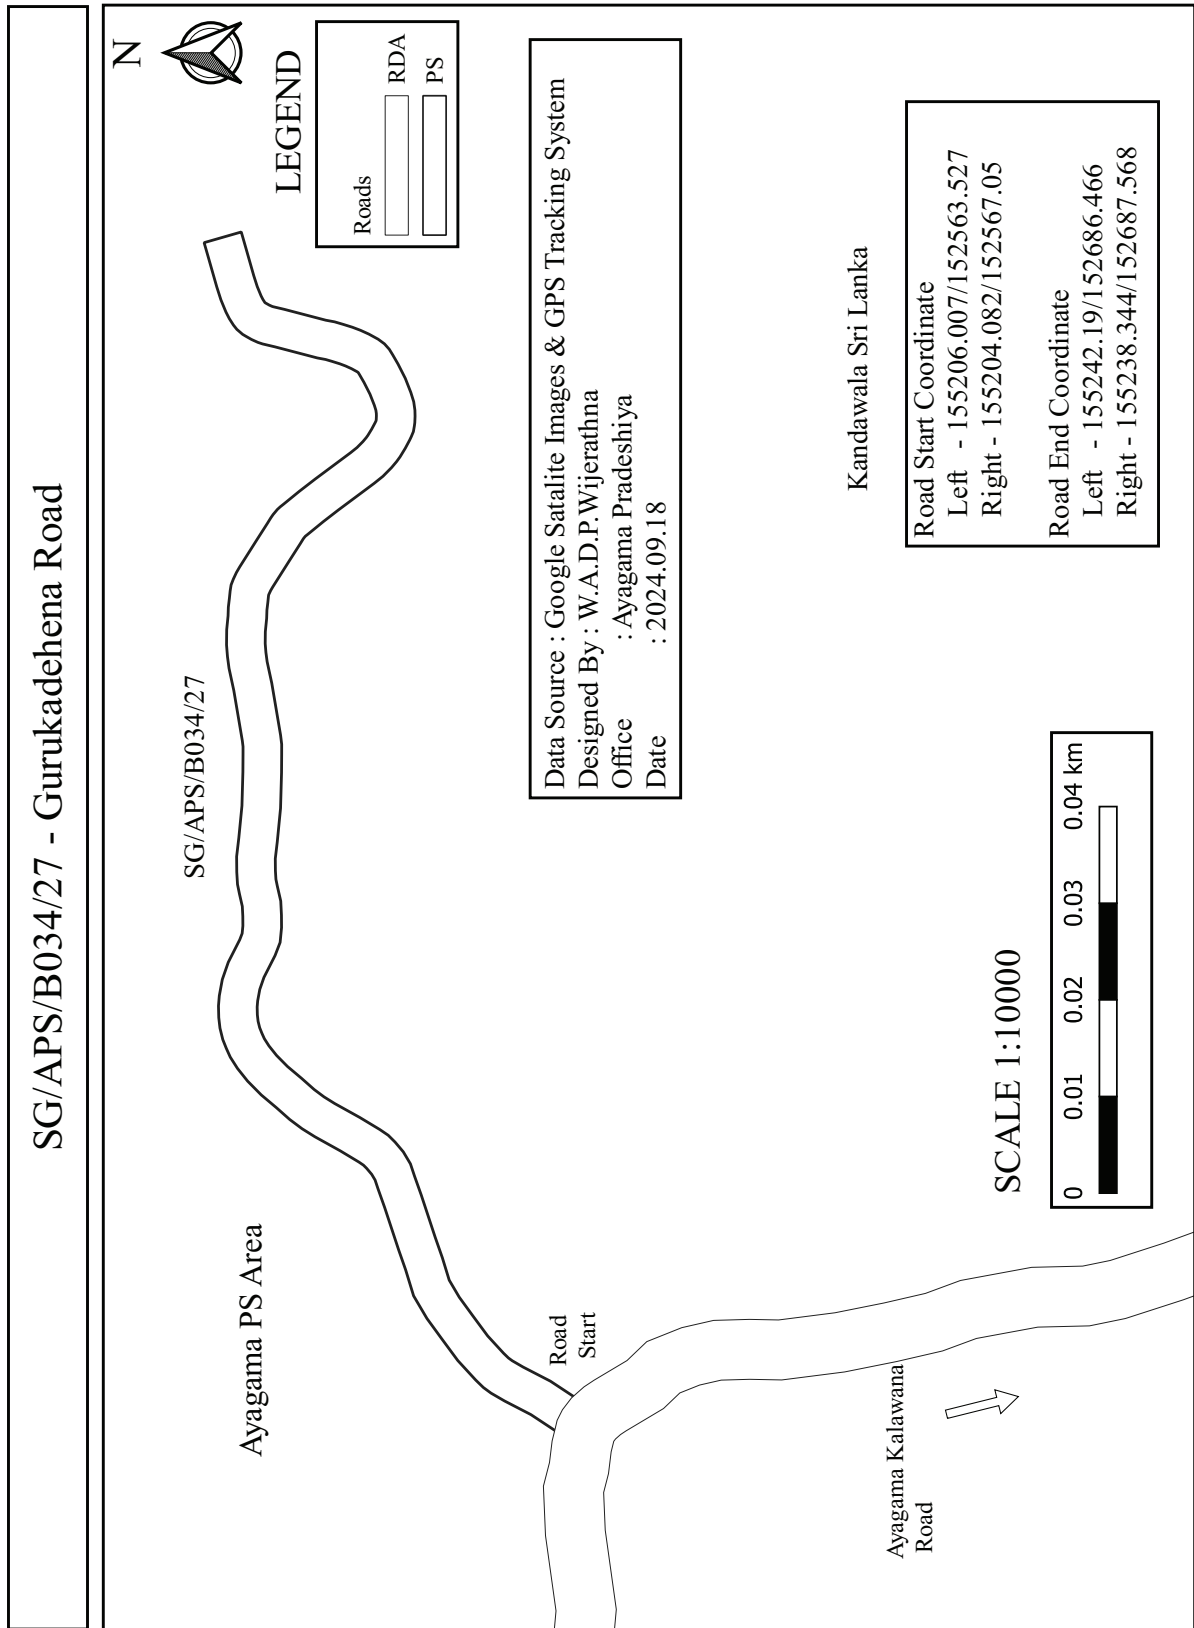


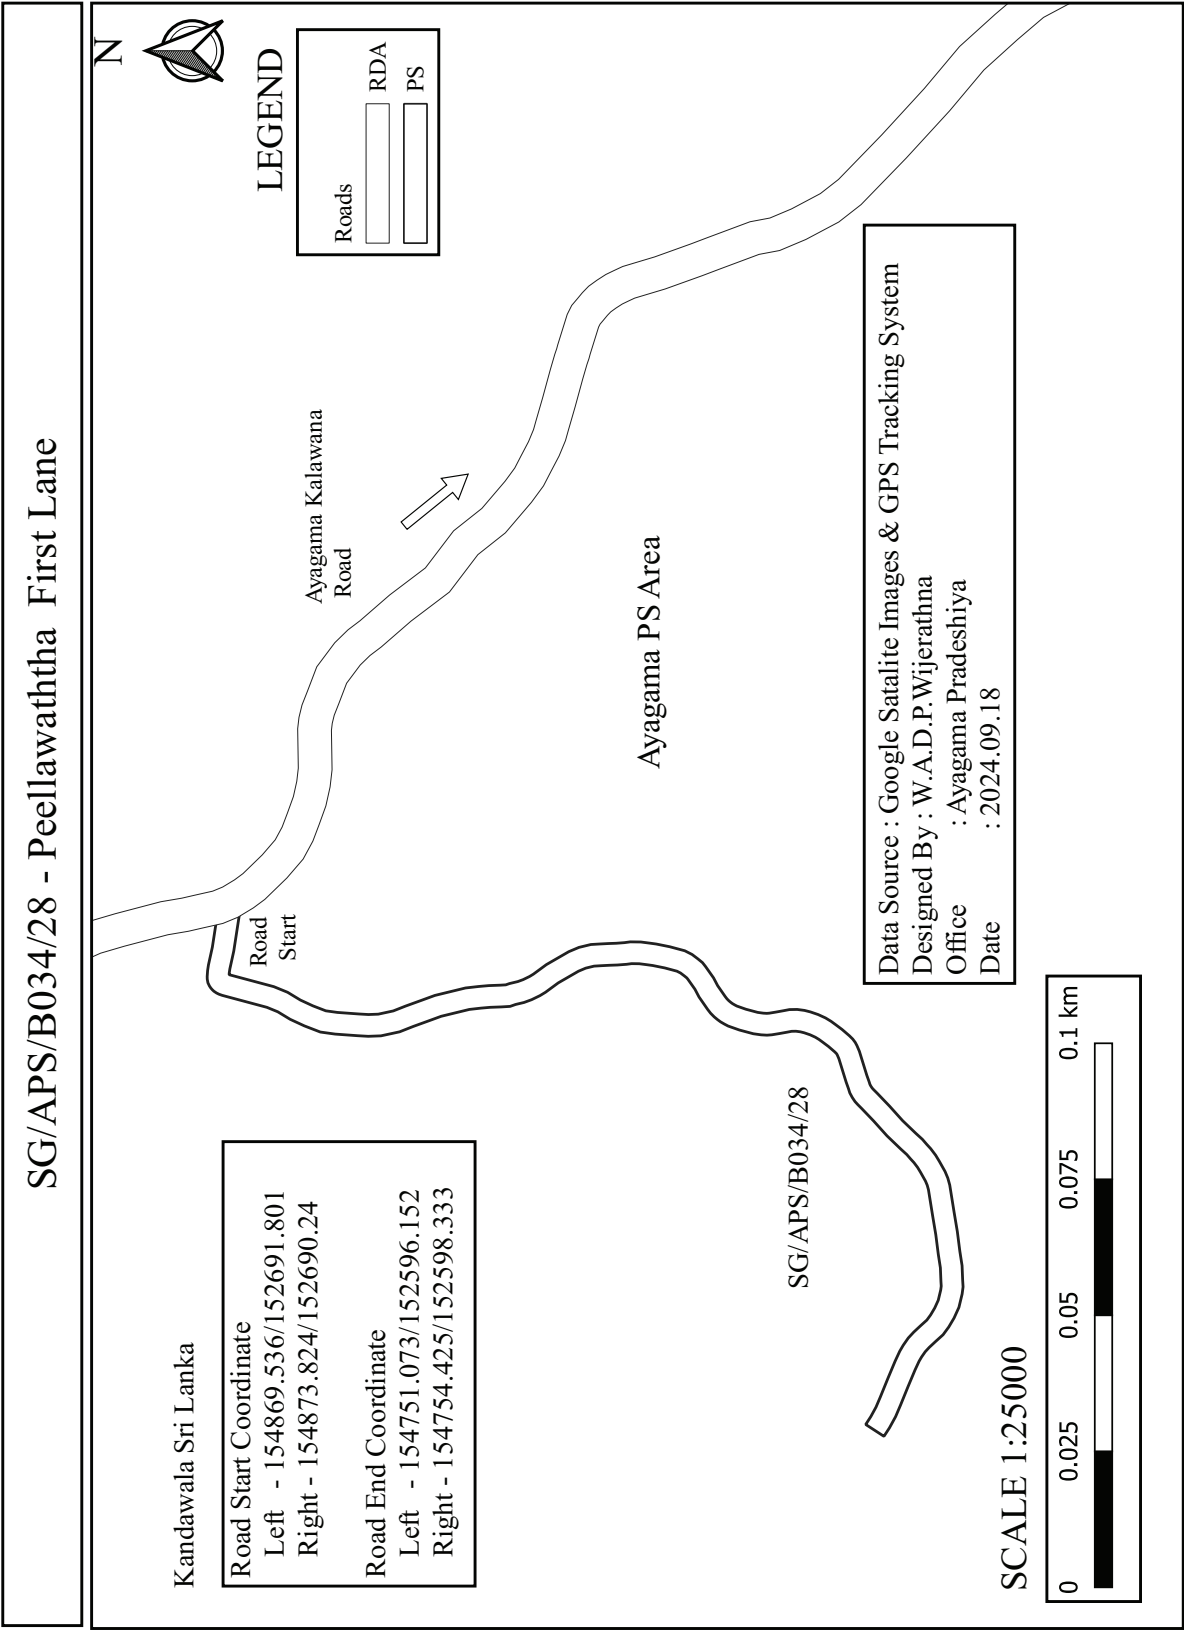


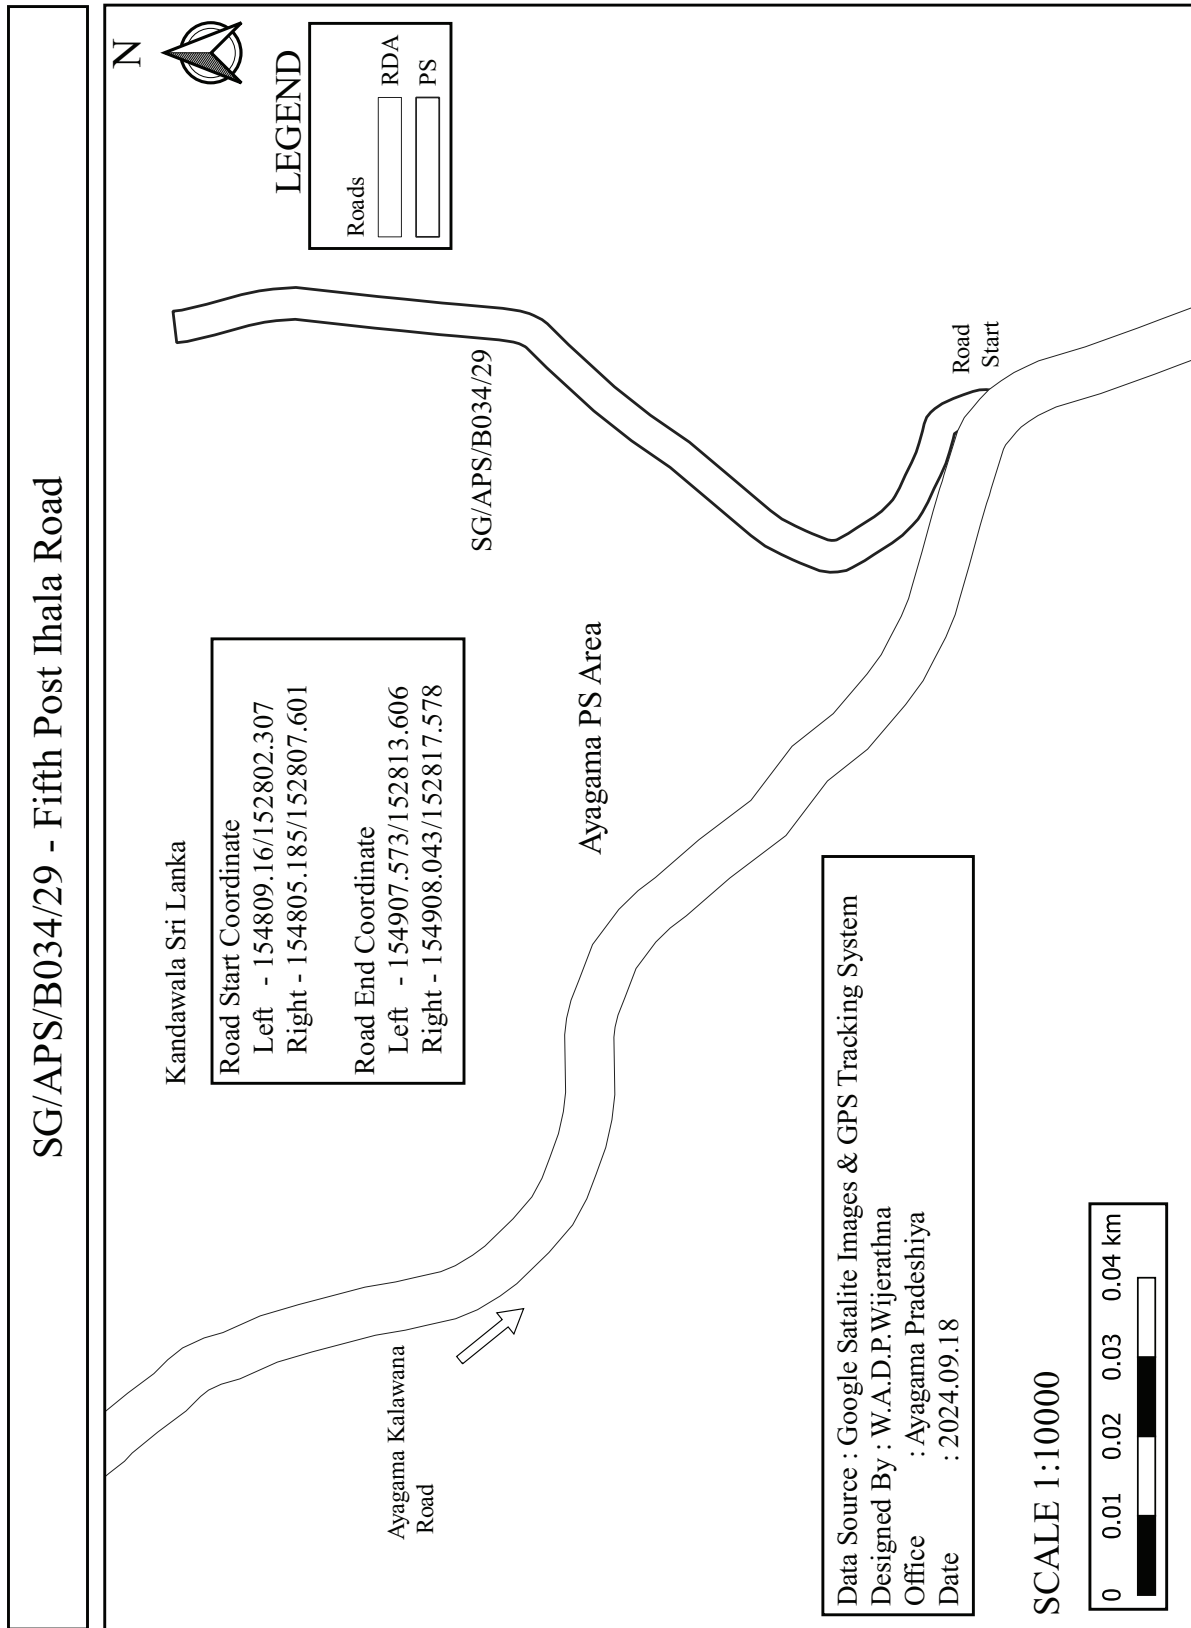


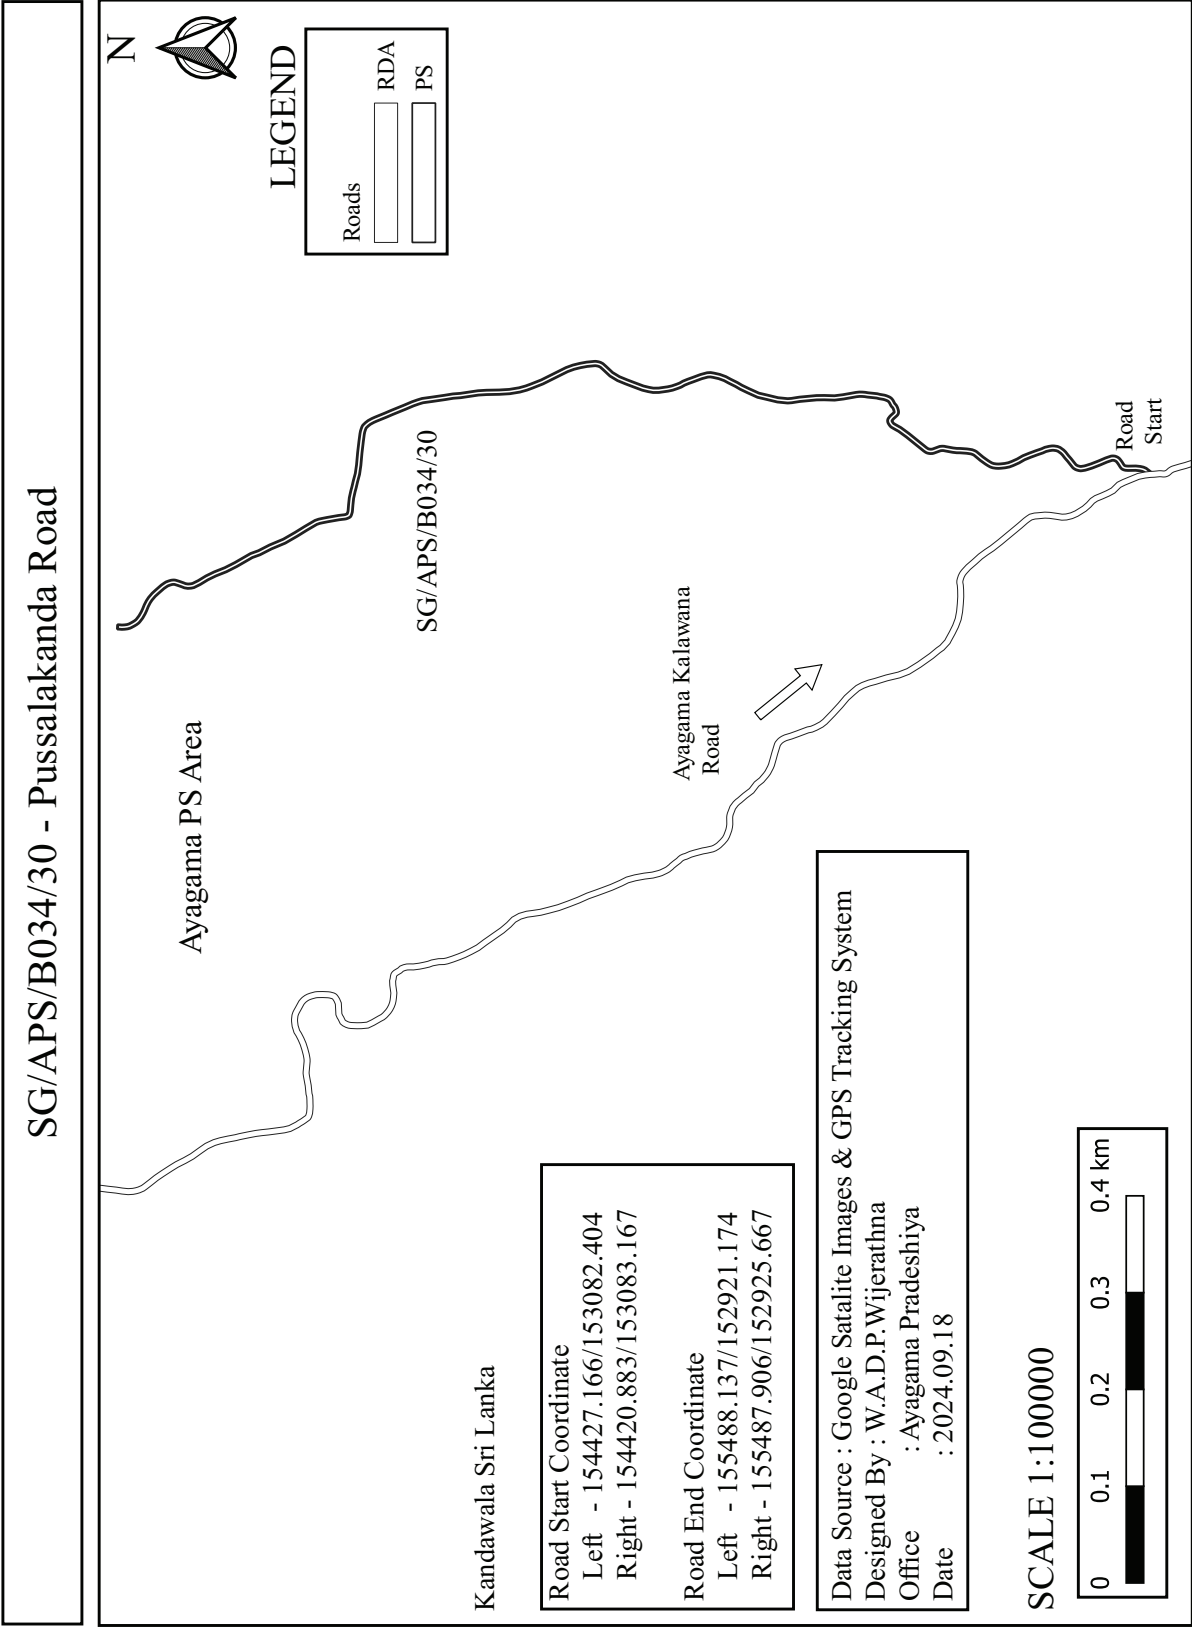


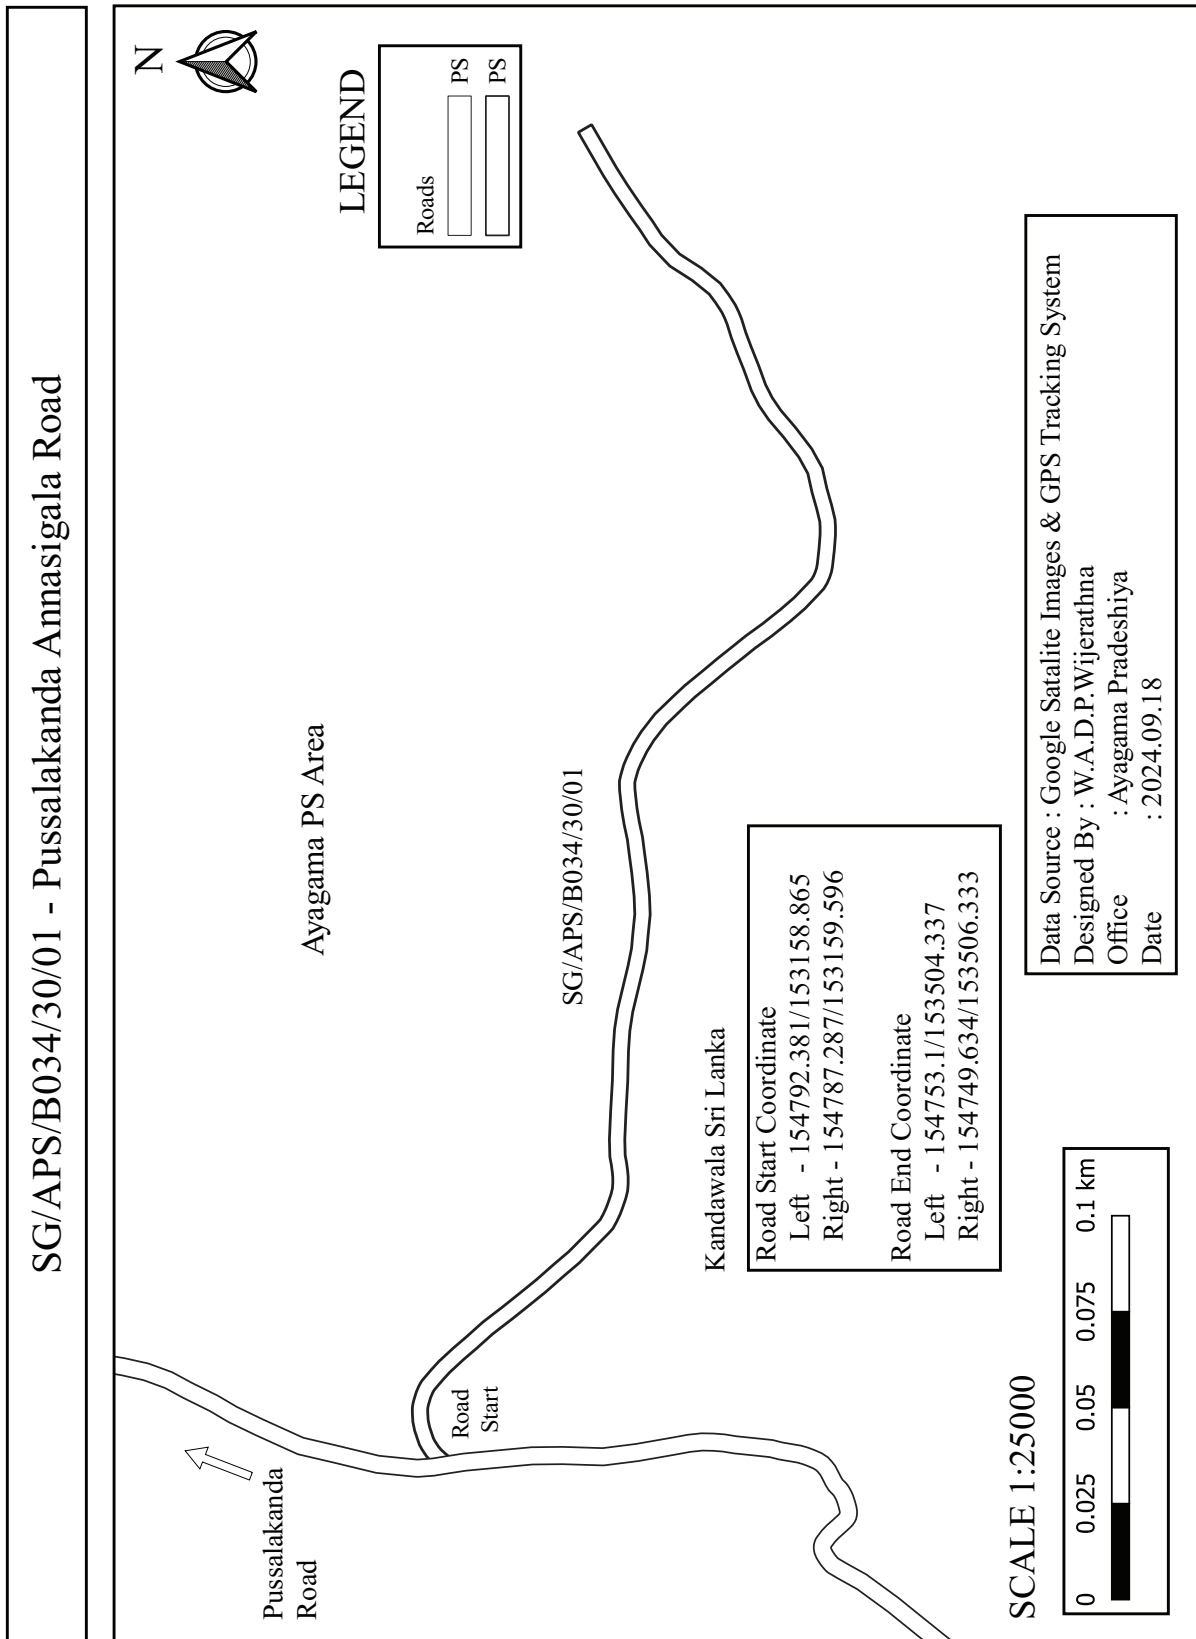


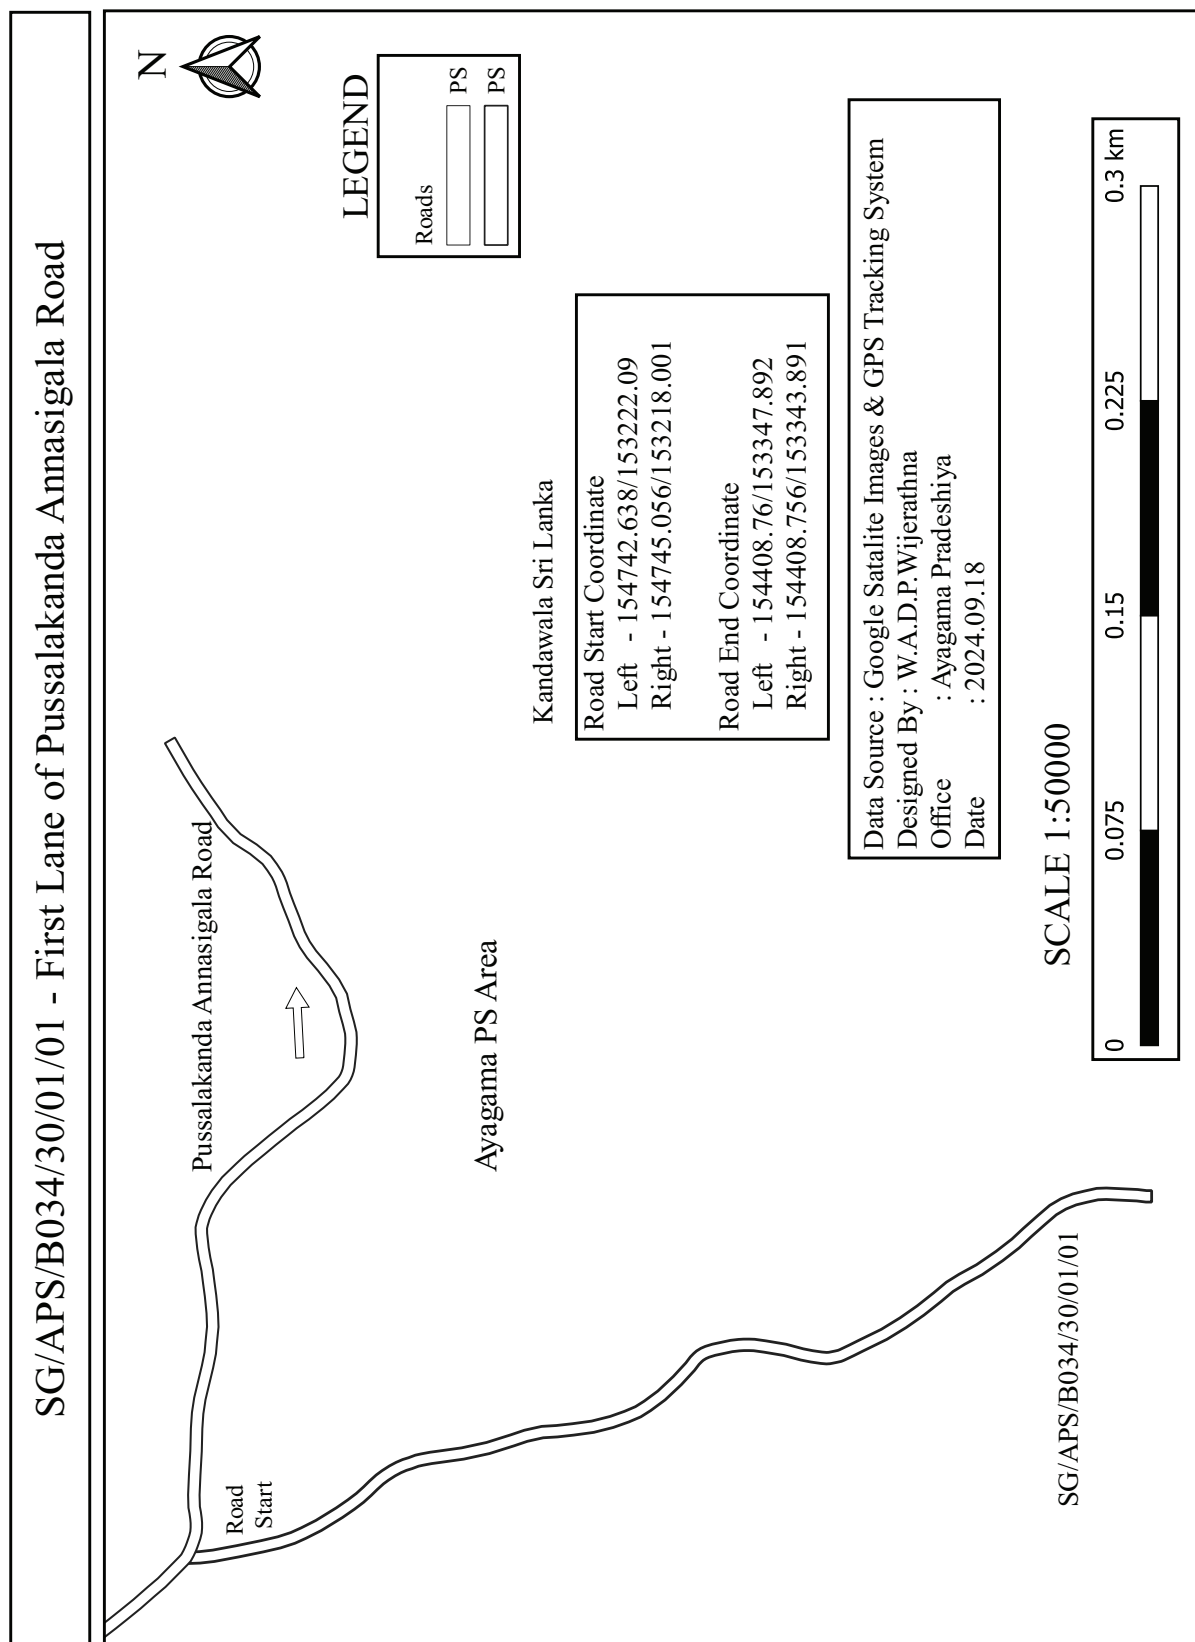


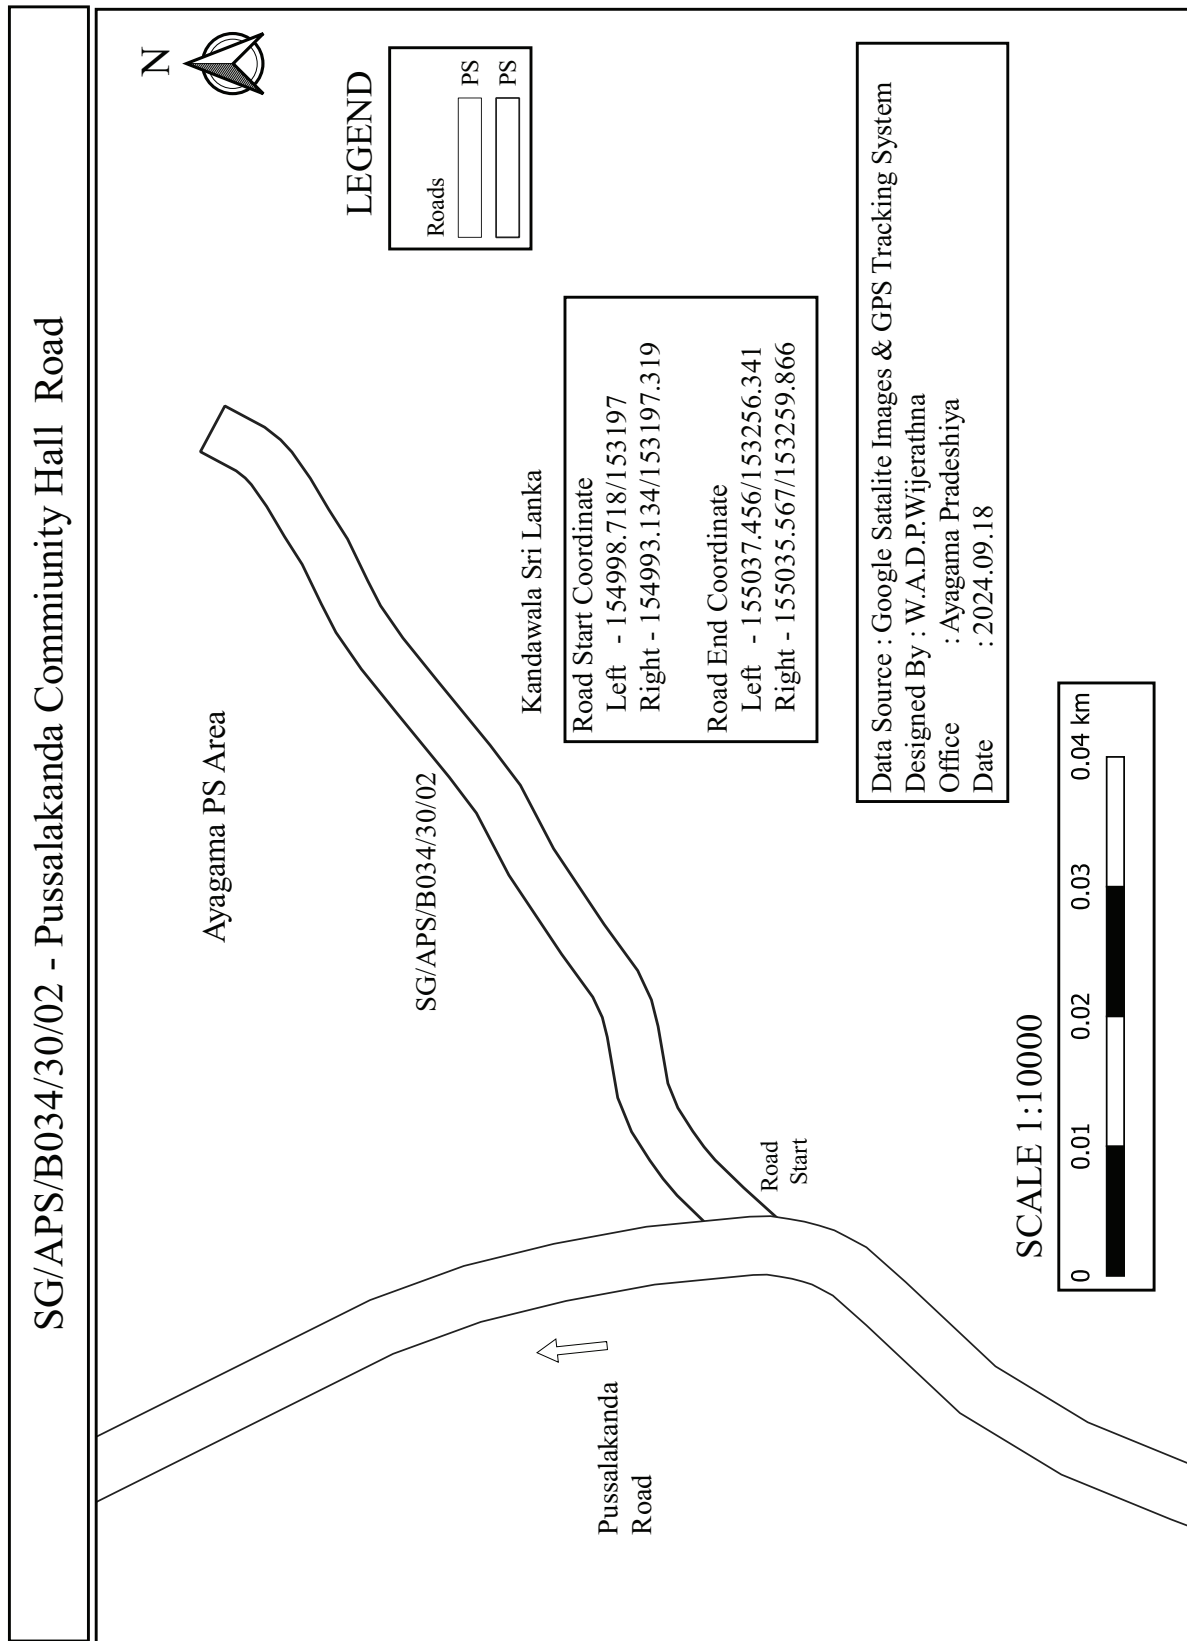


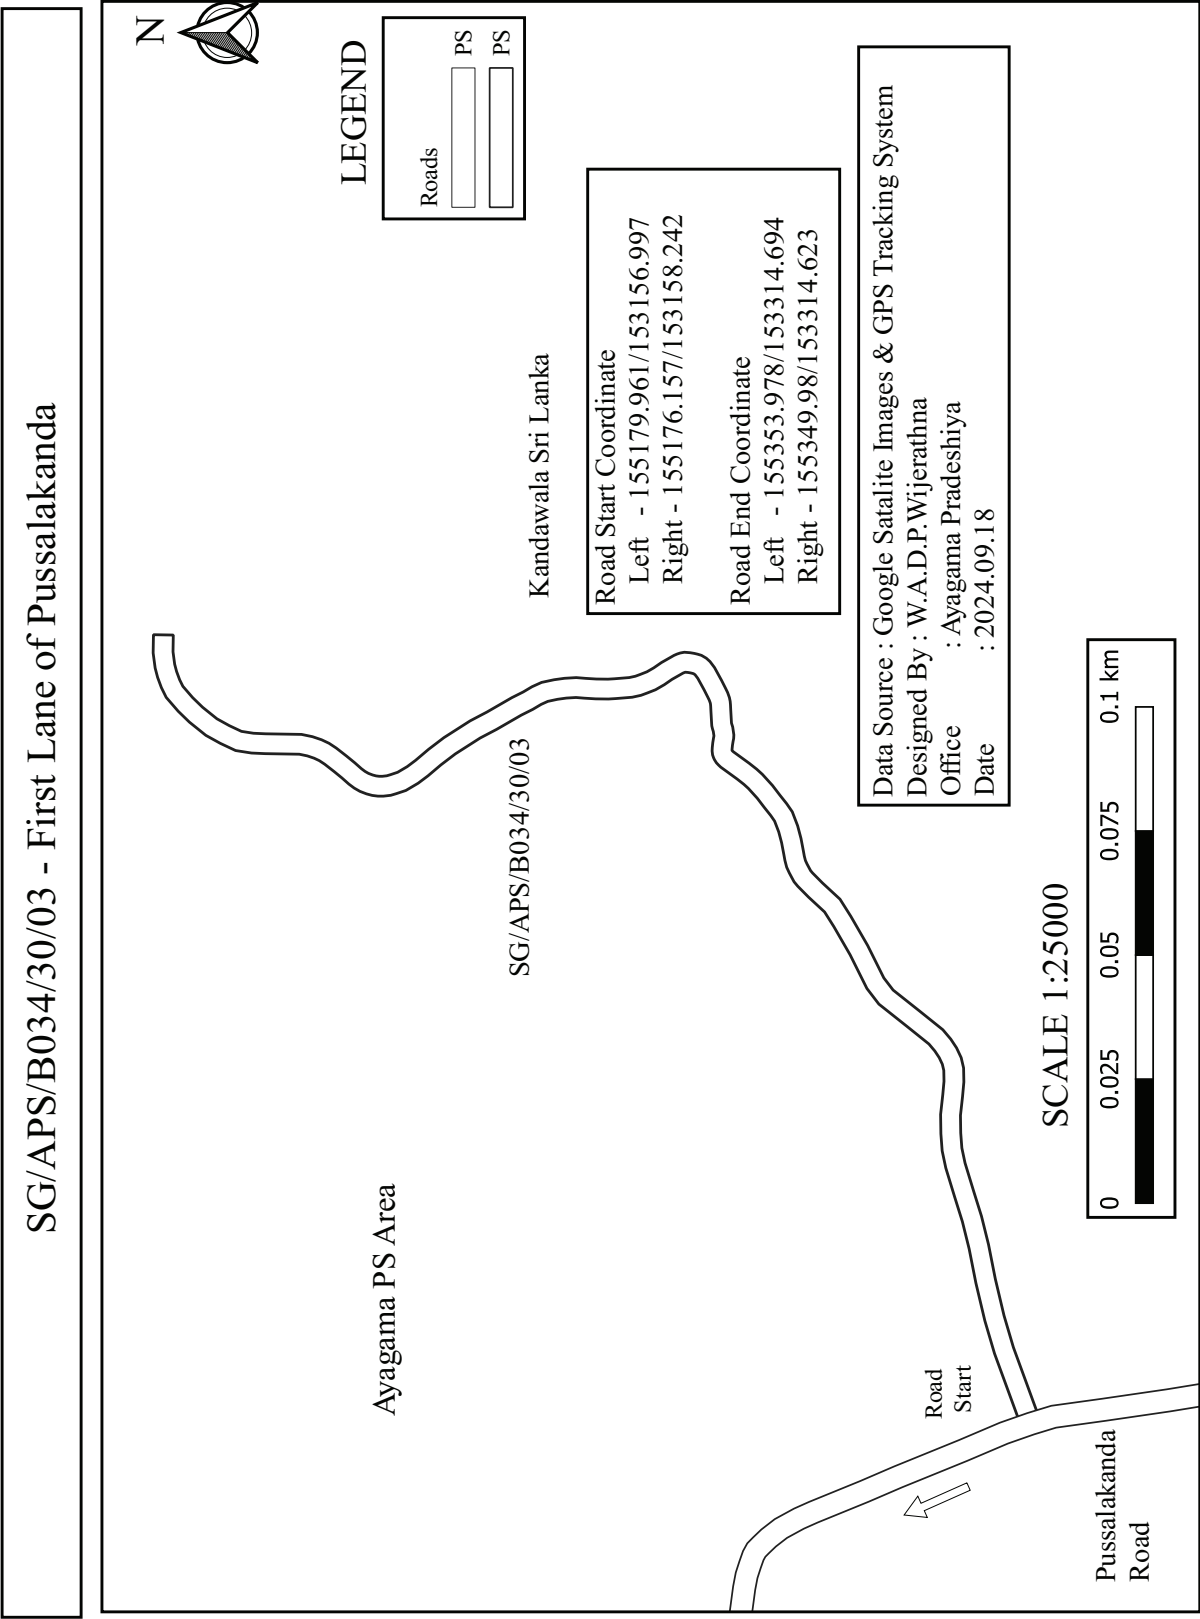


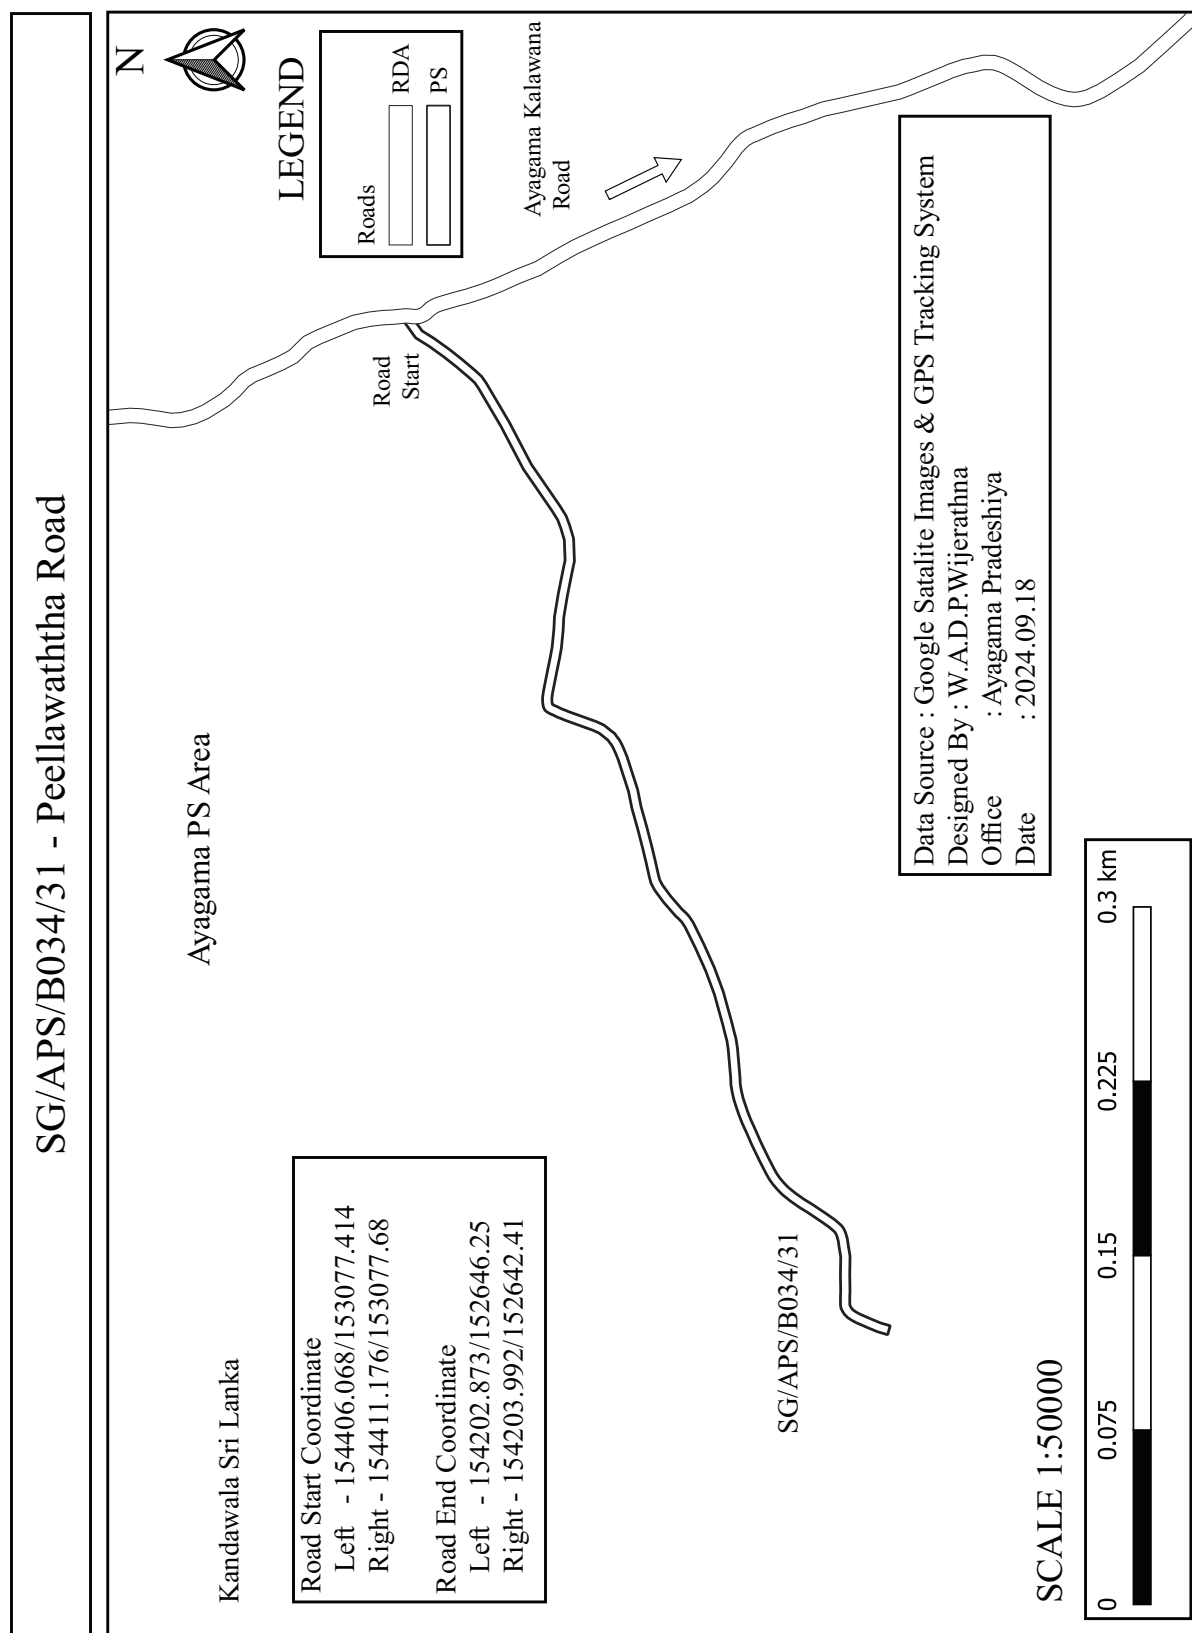


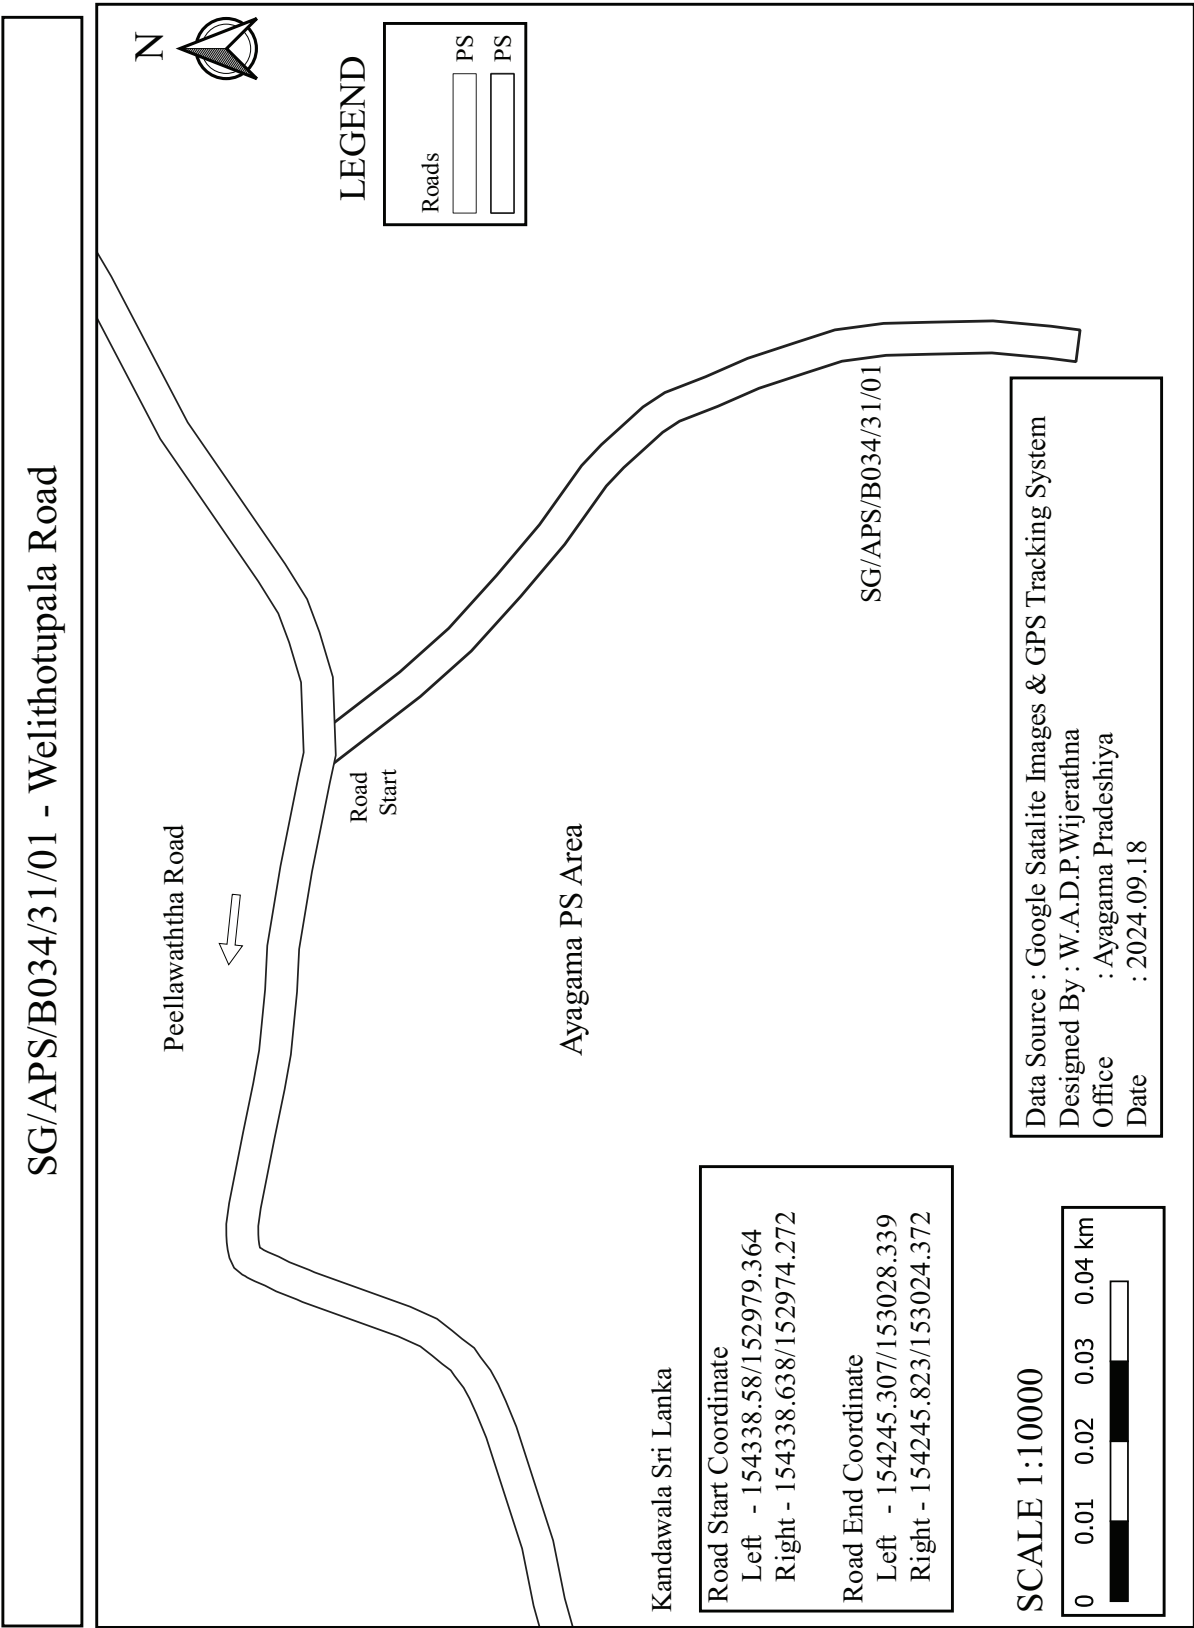


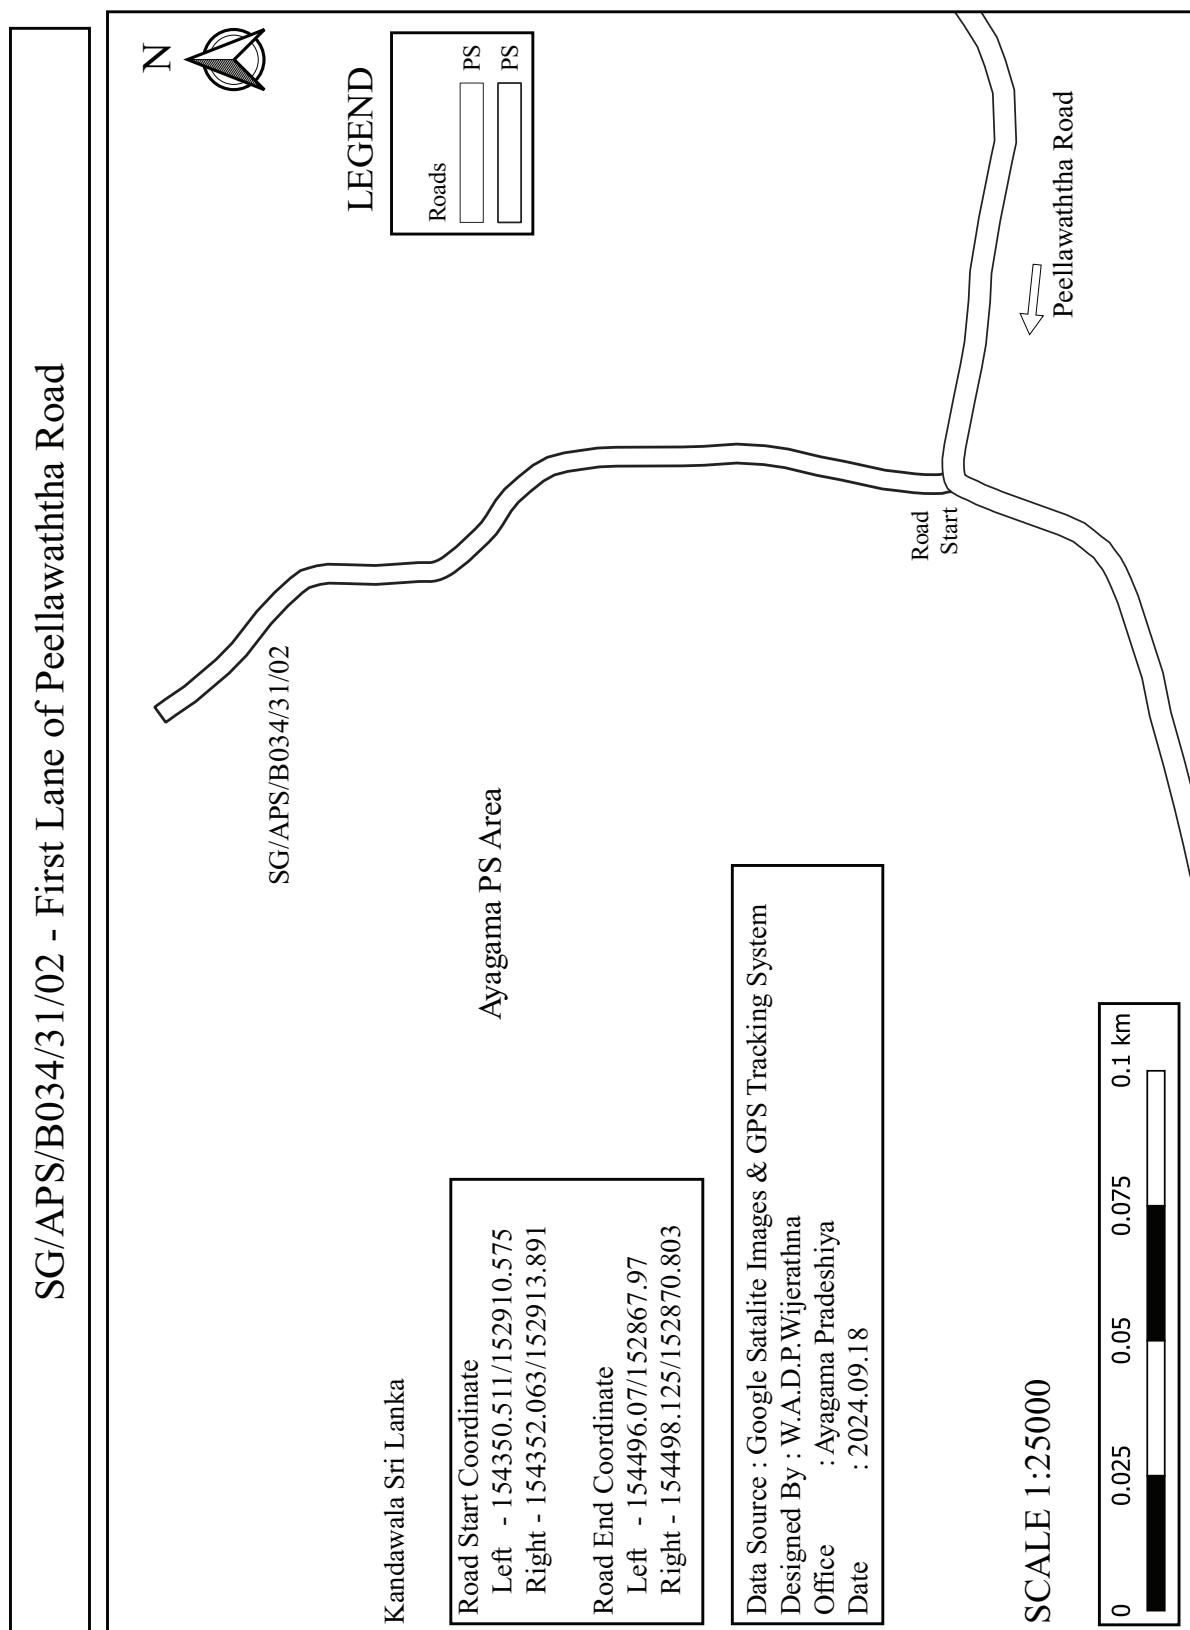


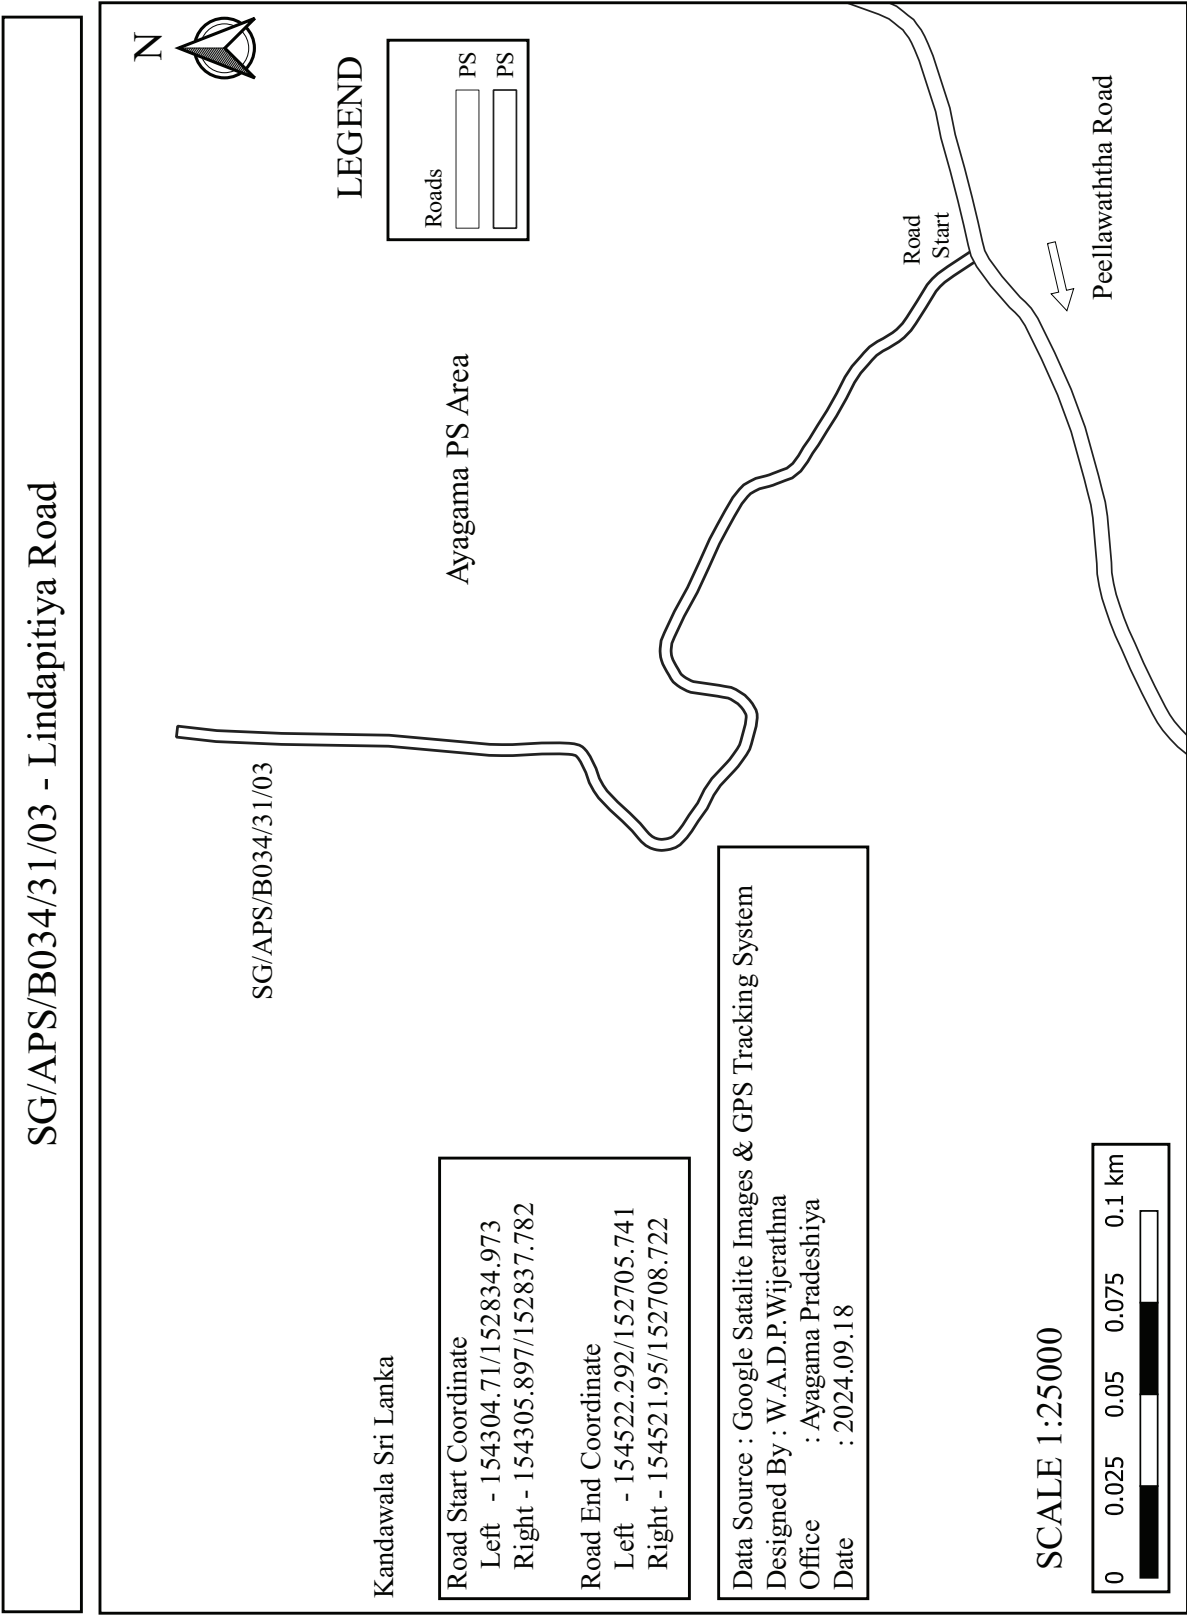


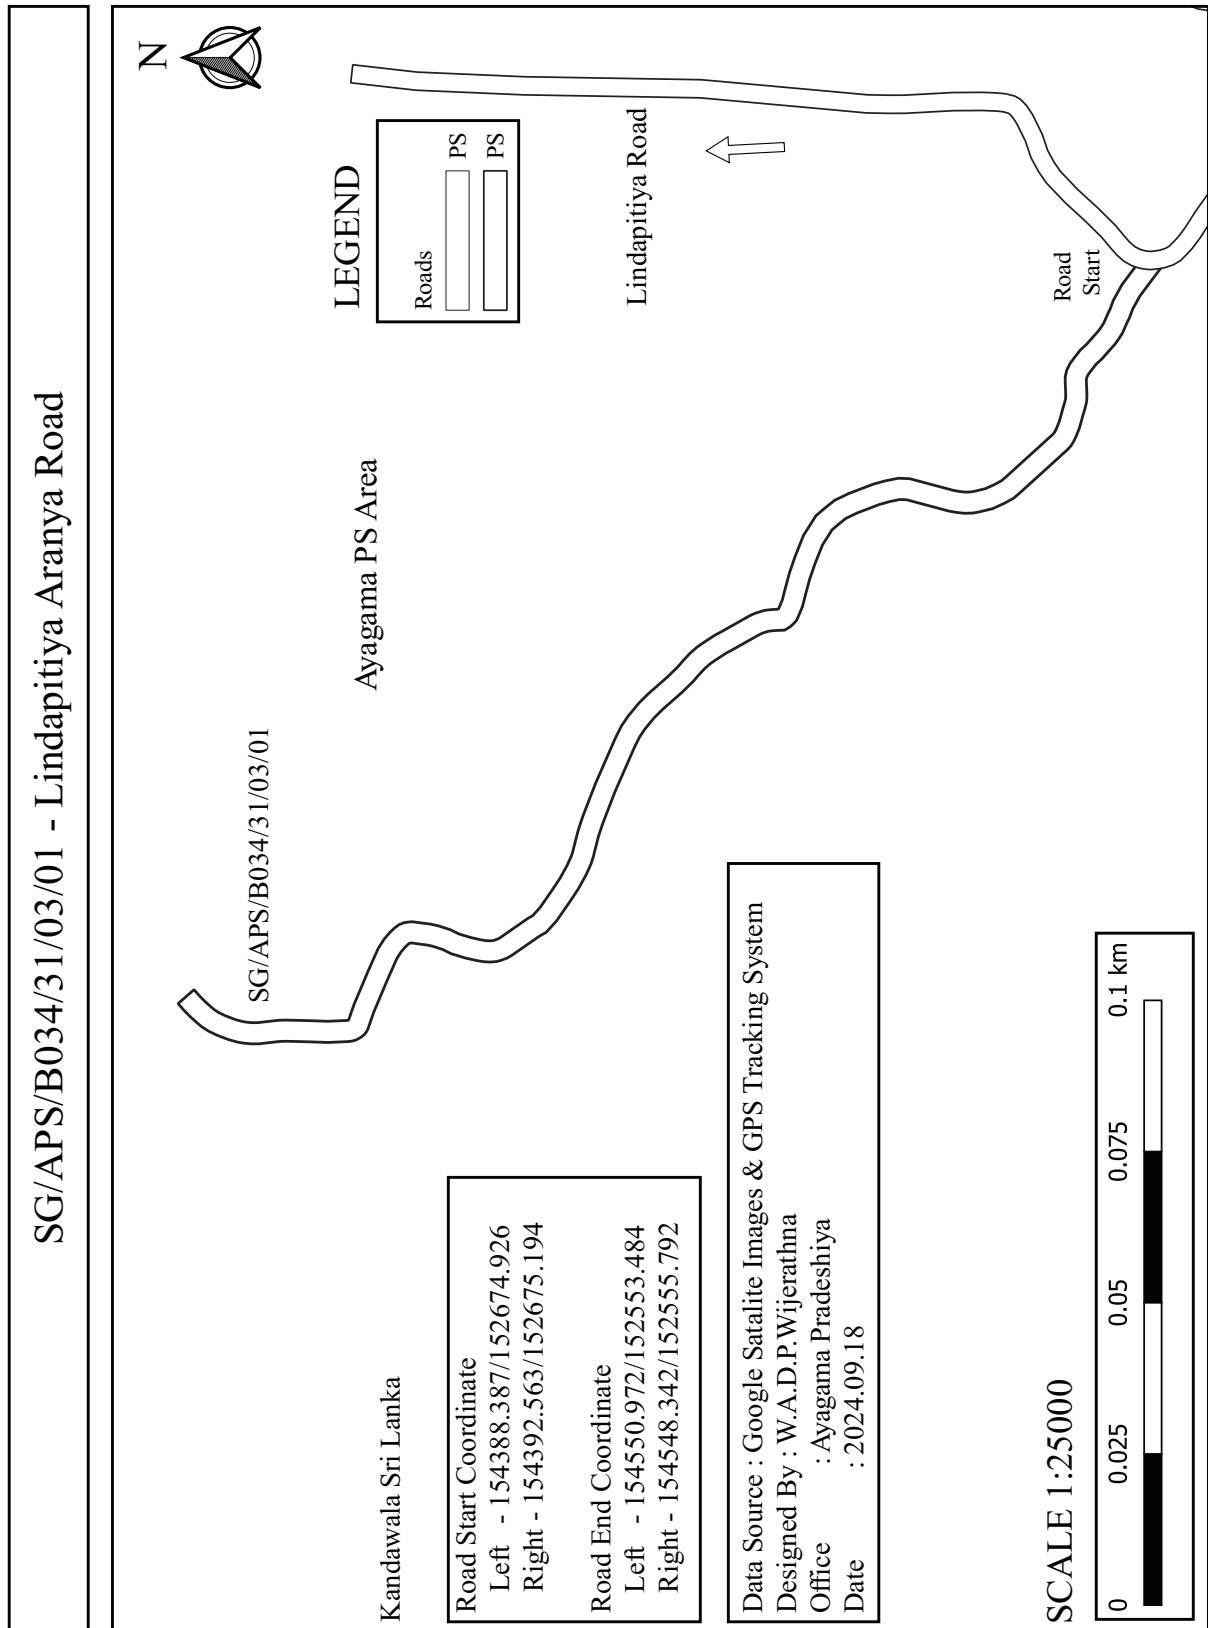


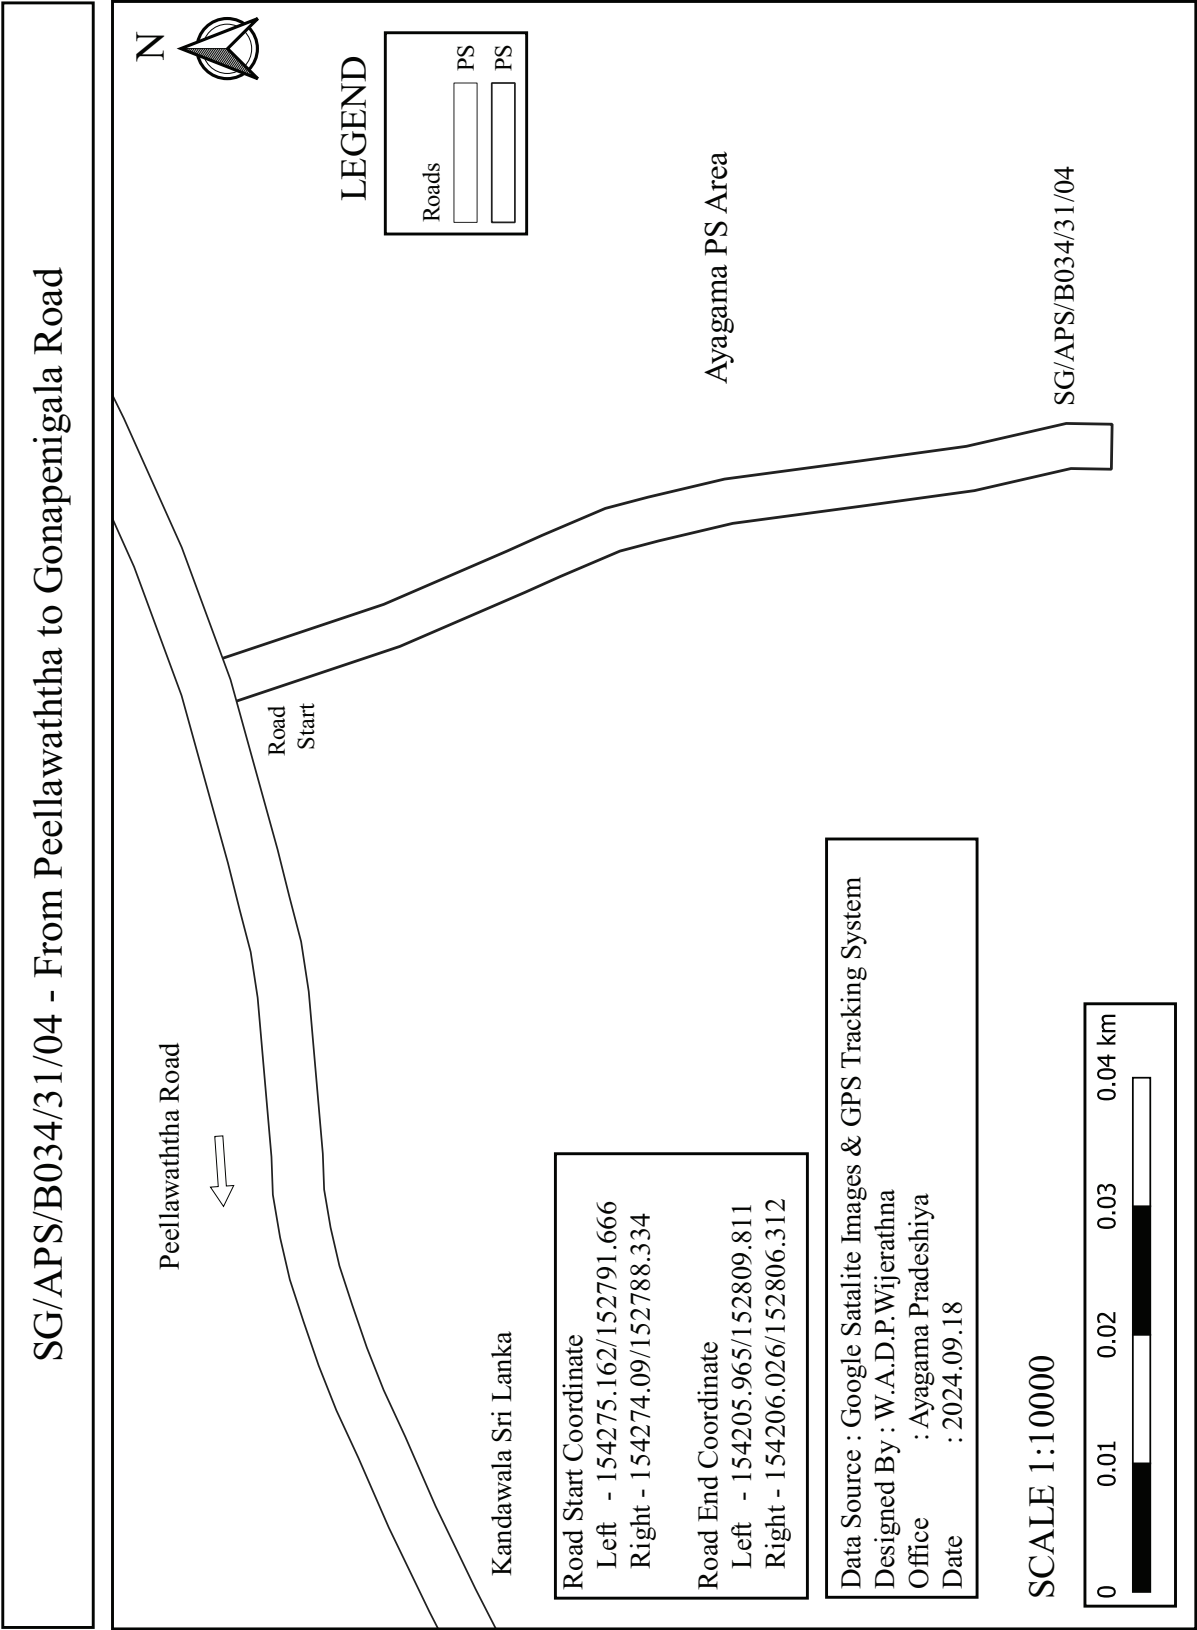


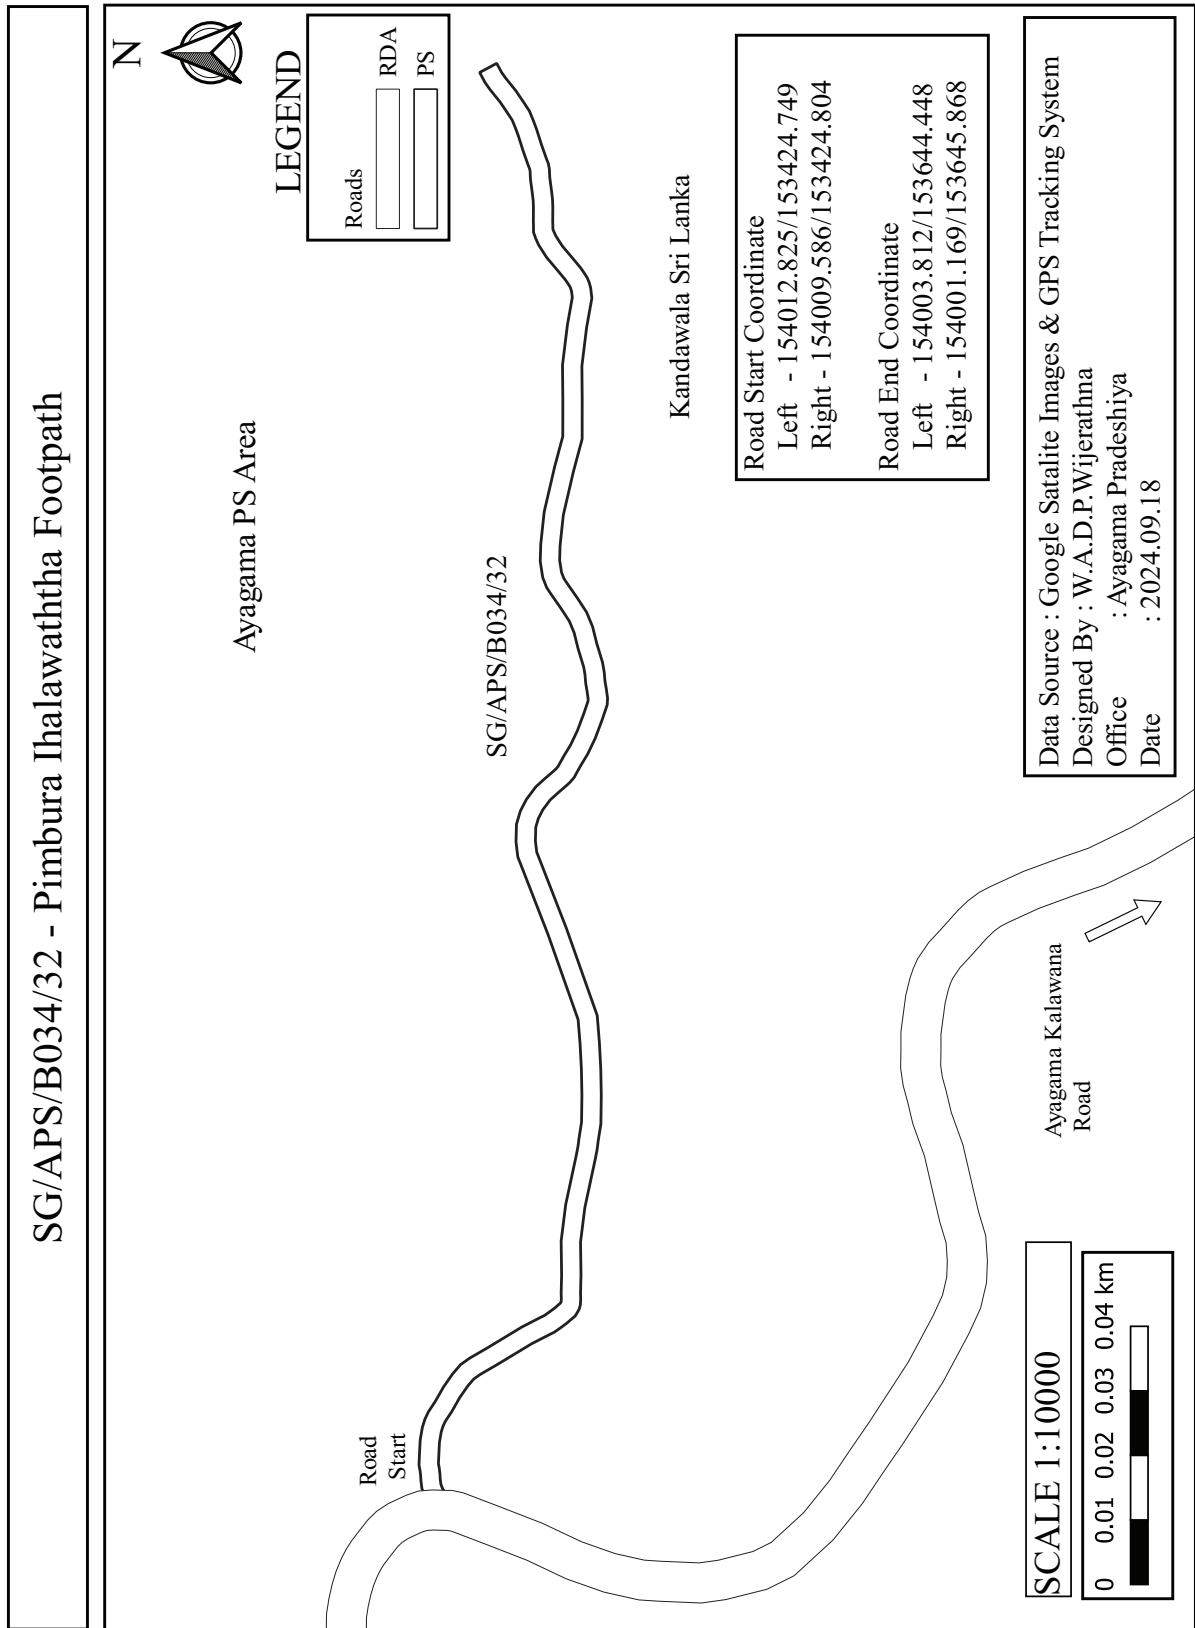


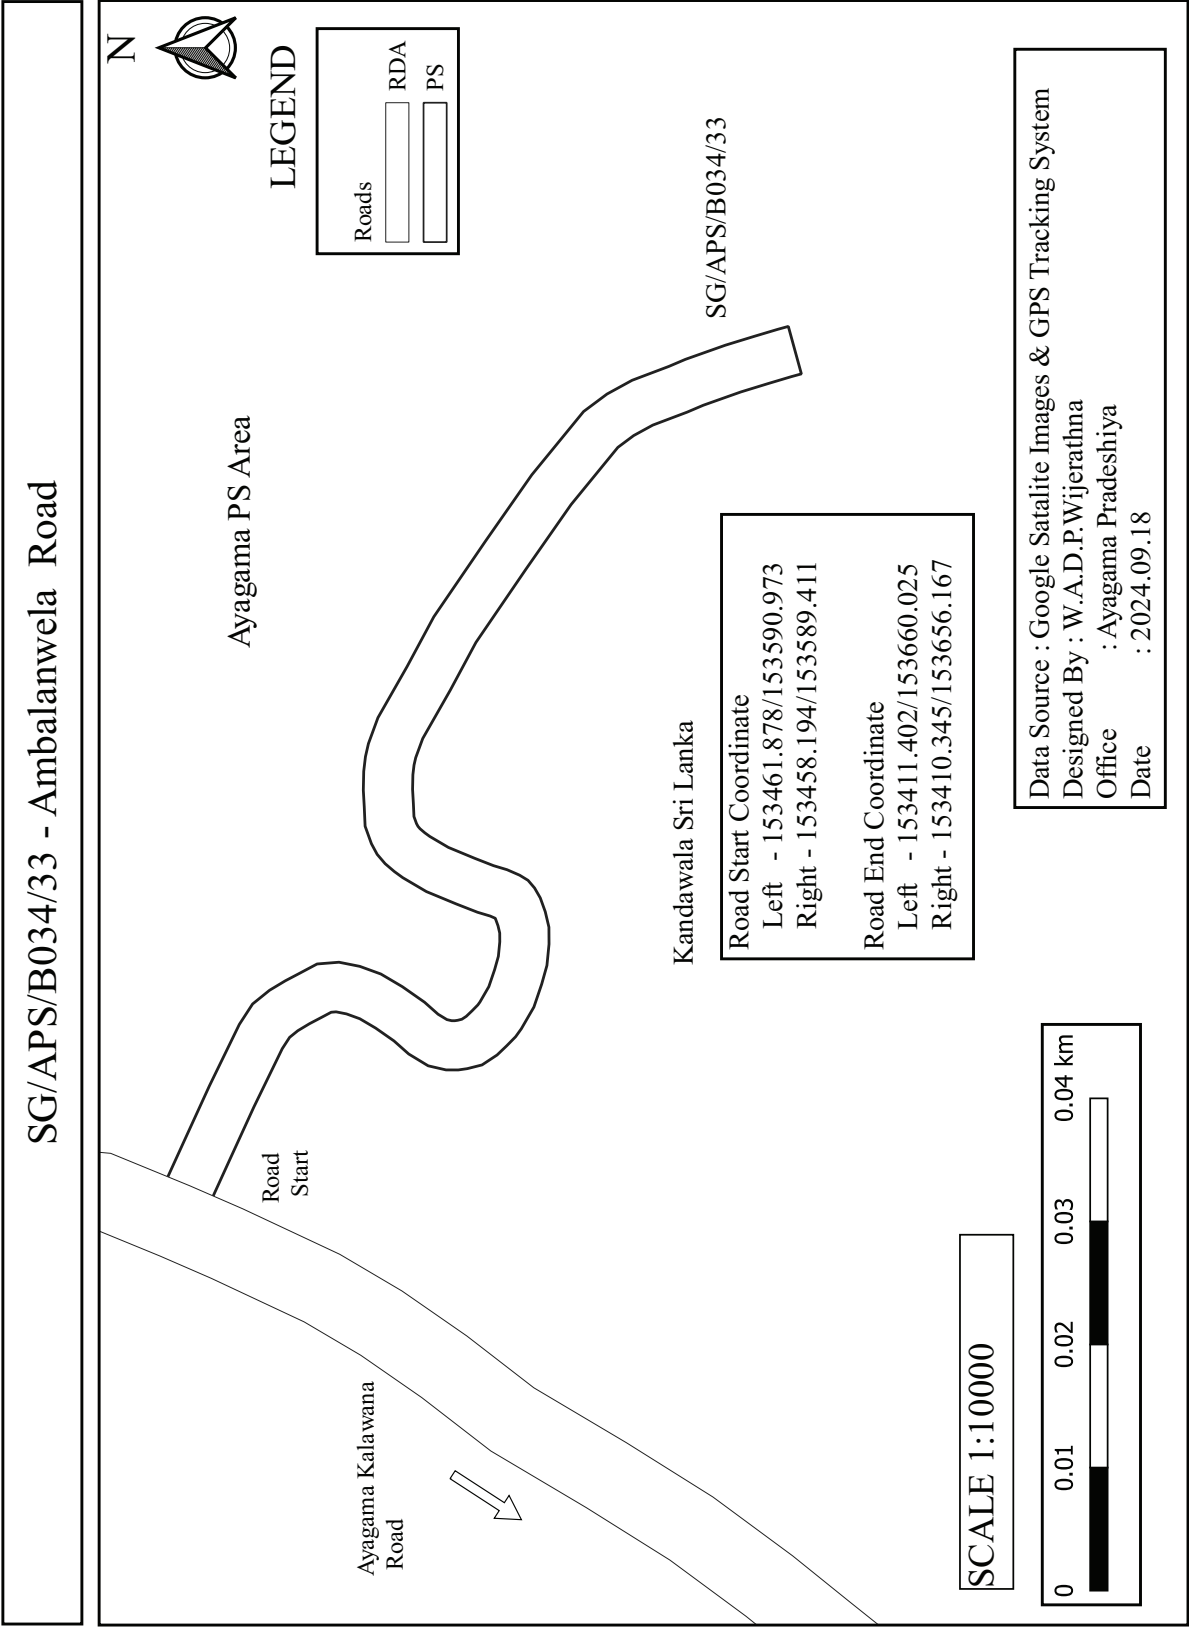

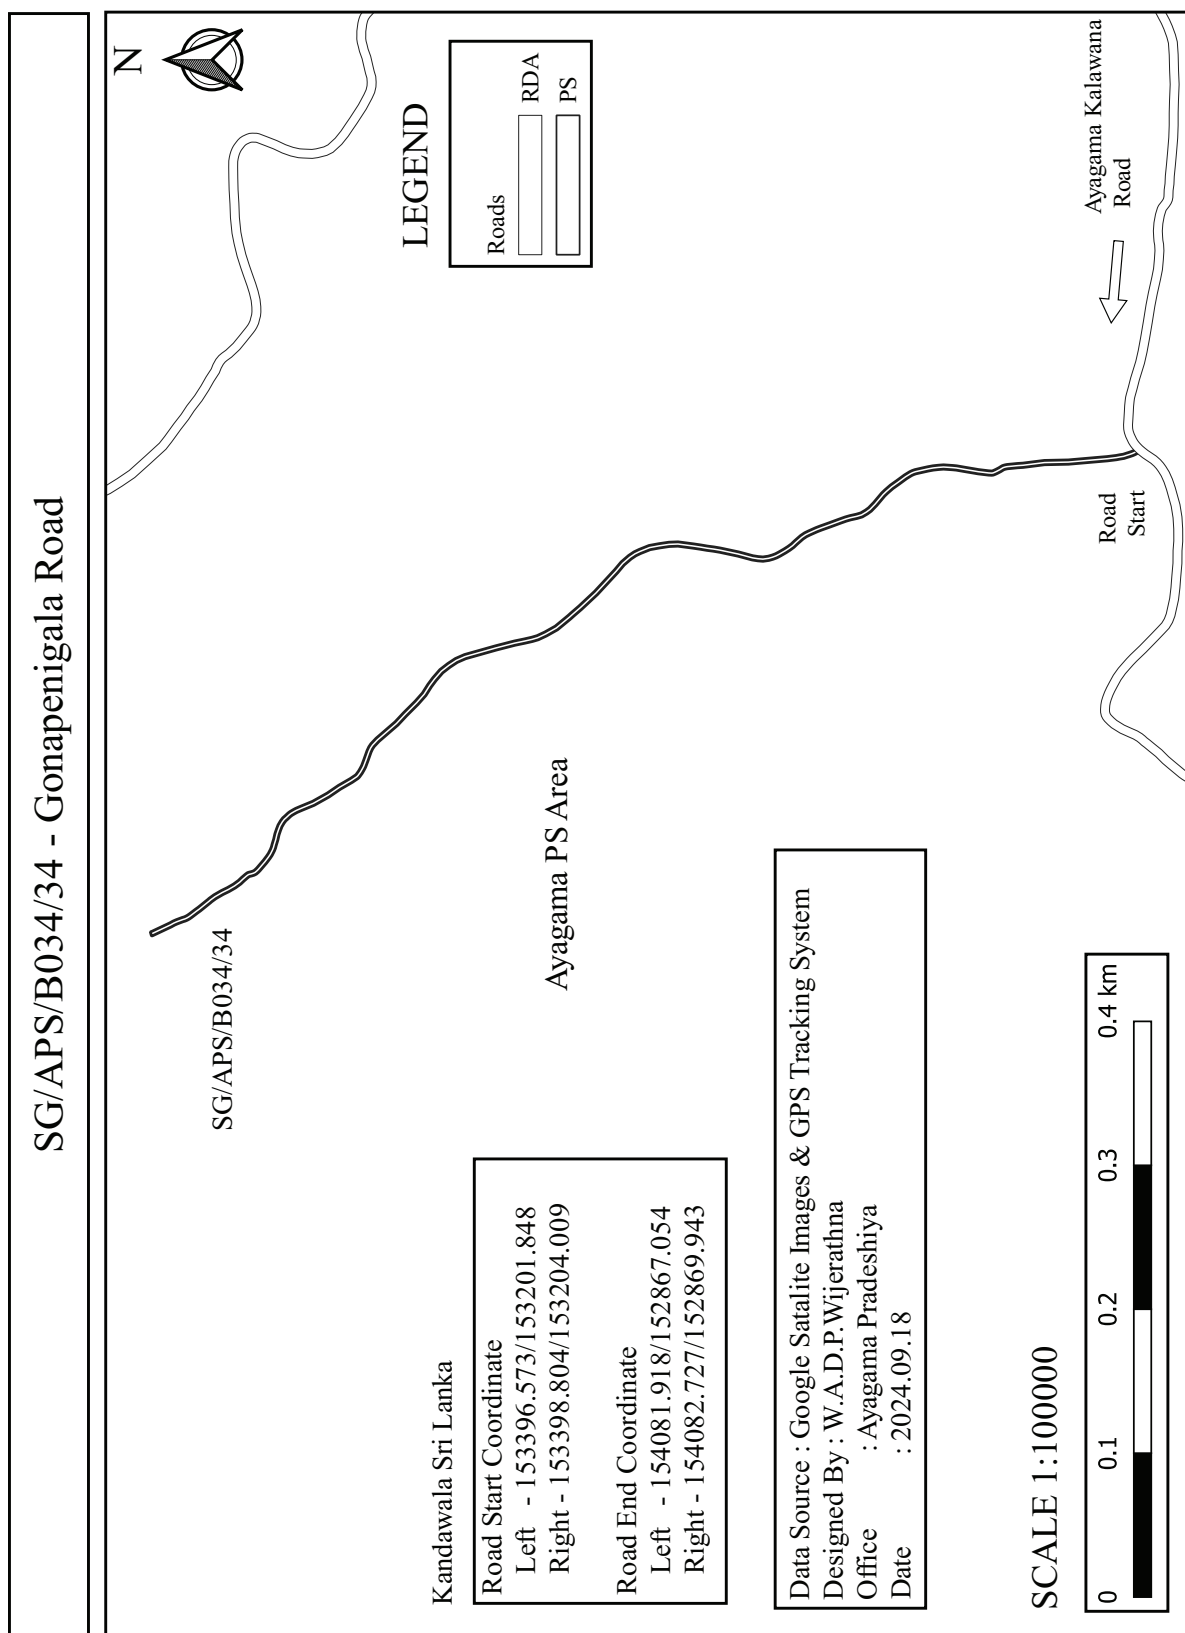


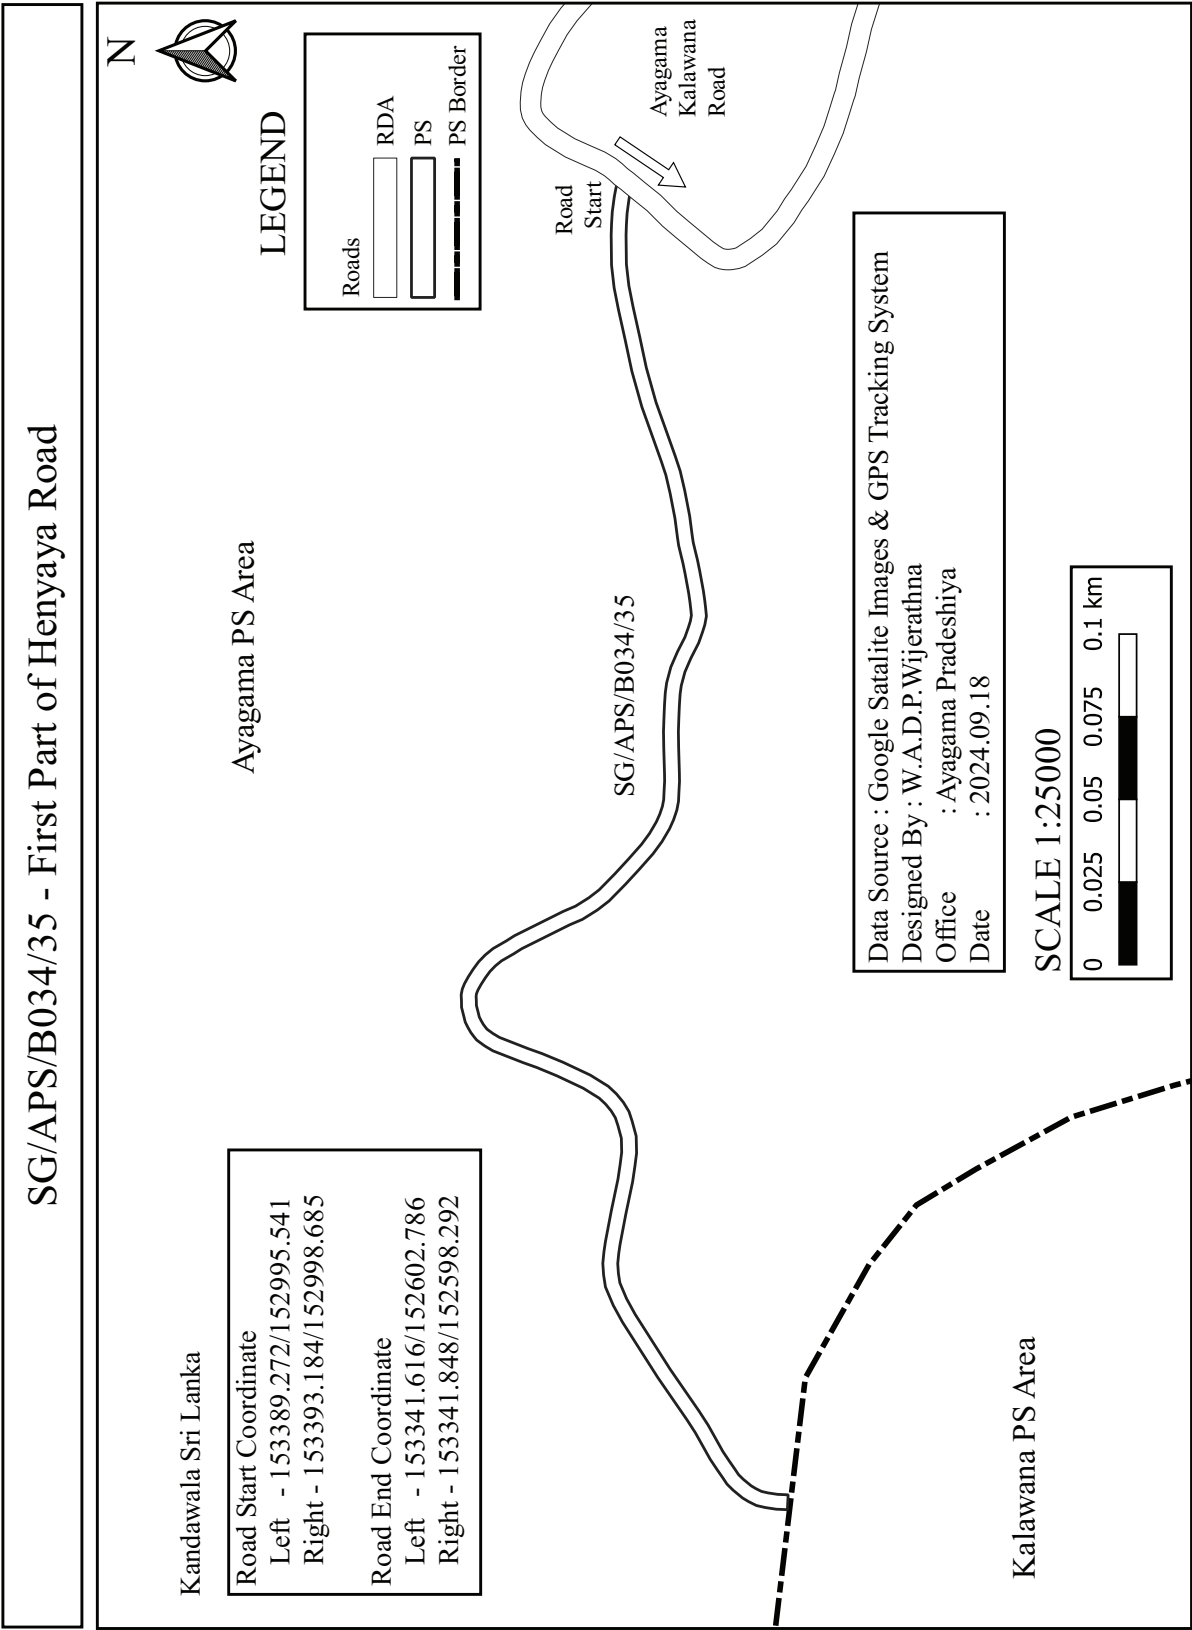

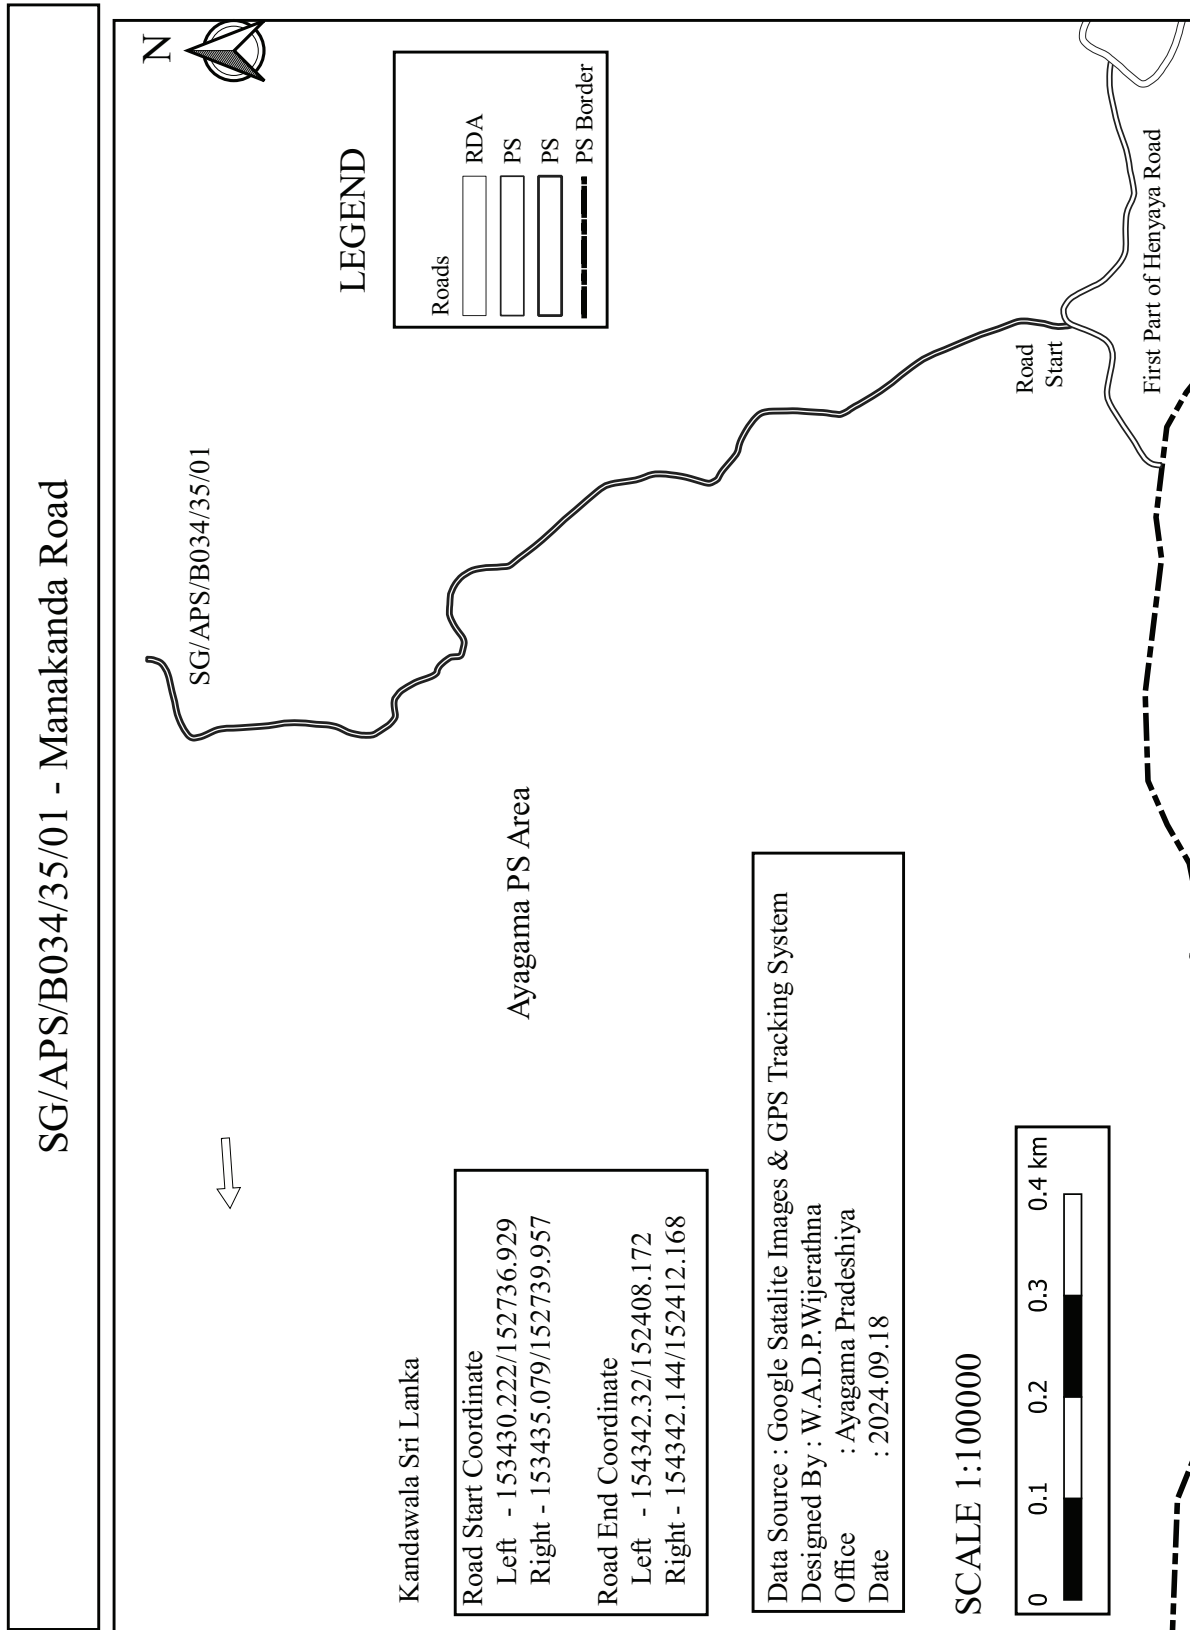


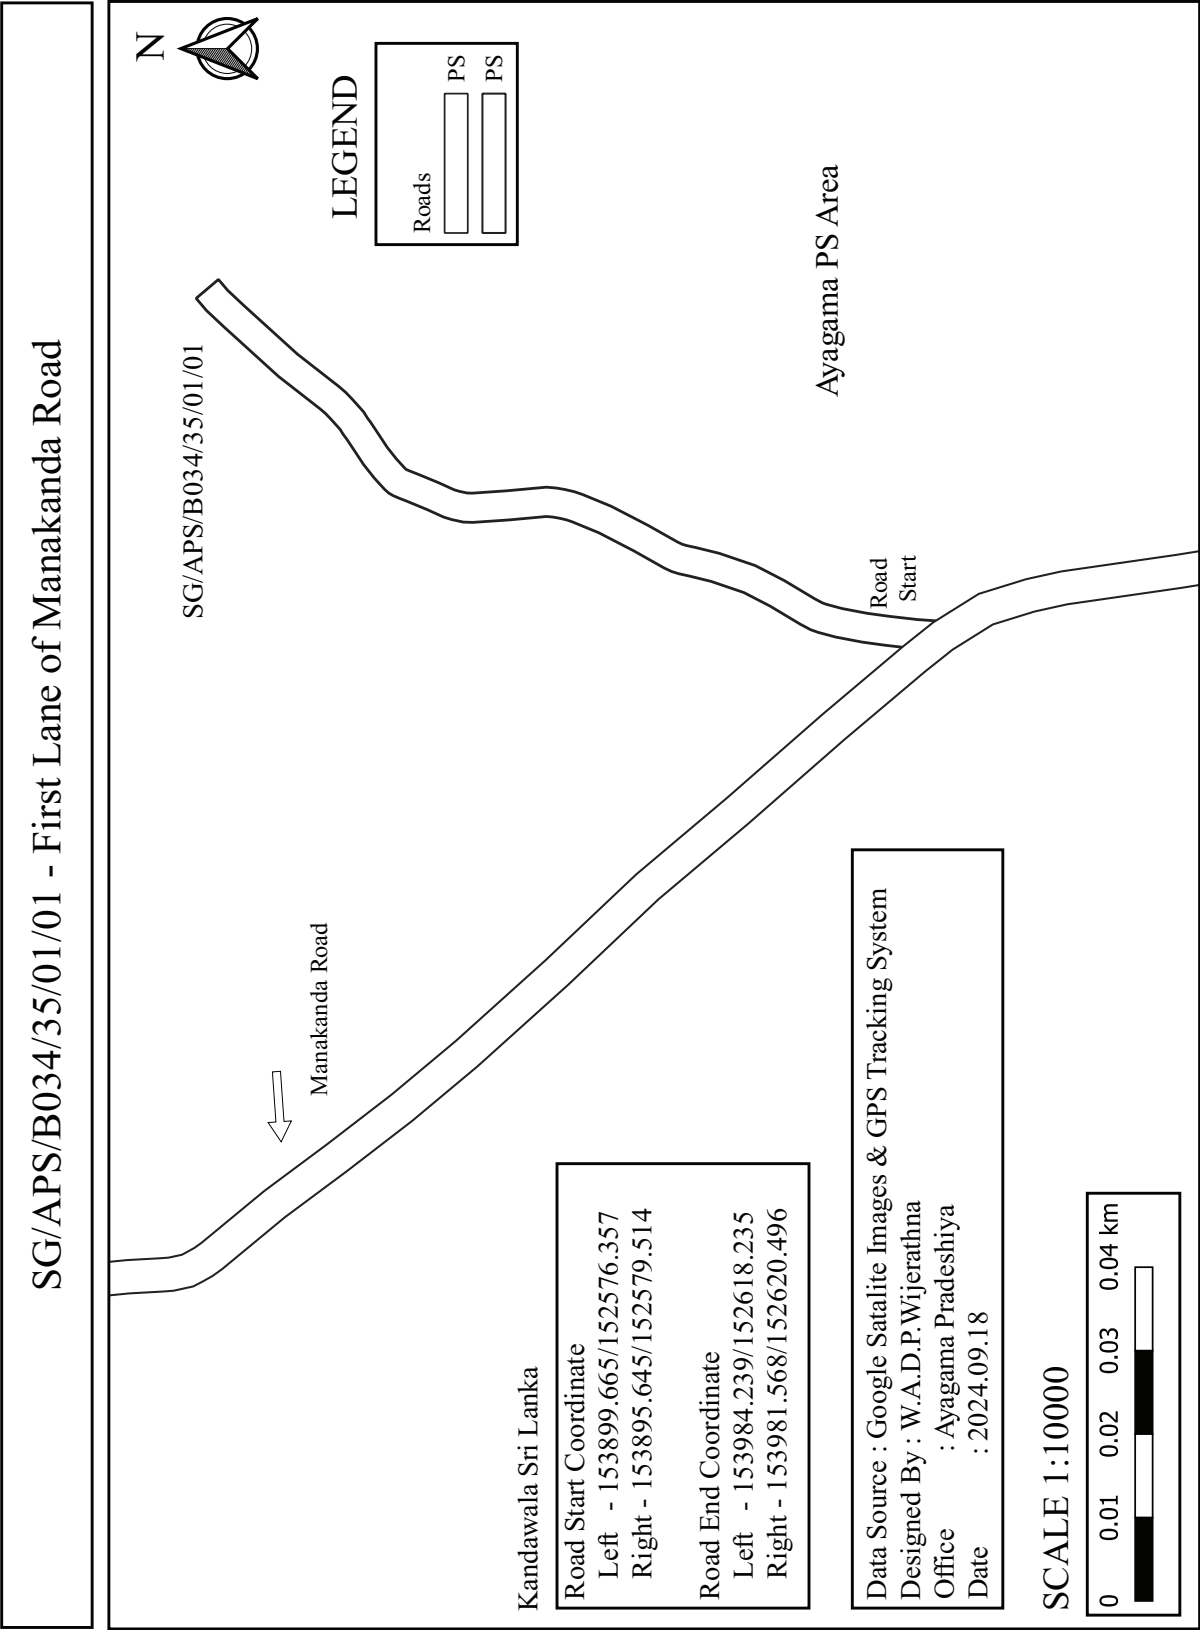



SG/APS/B034/35/01/02 - Second Lane of Manakanda Road

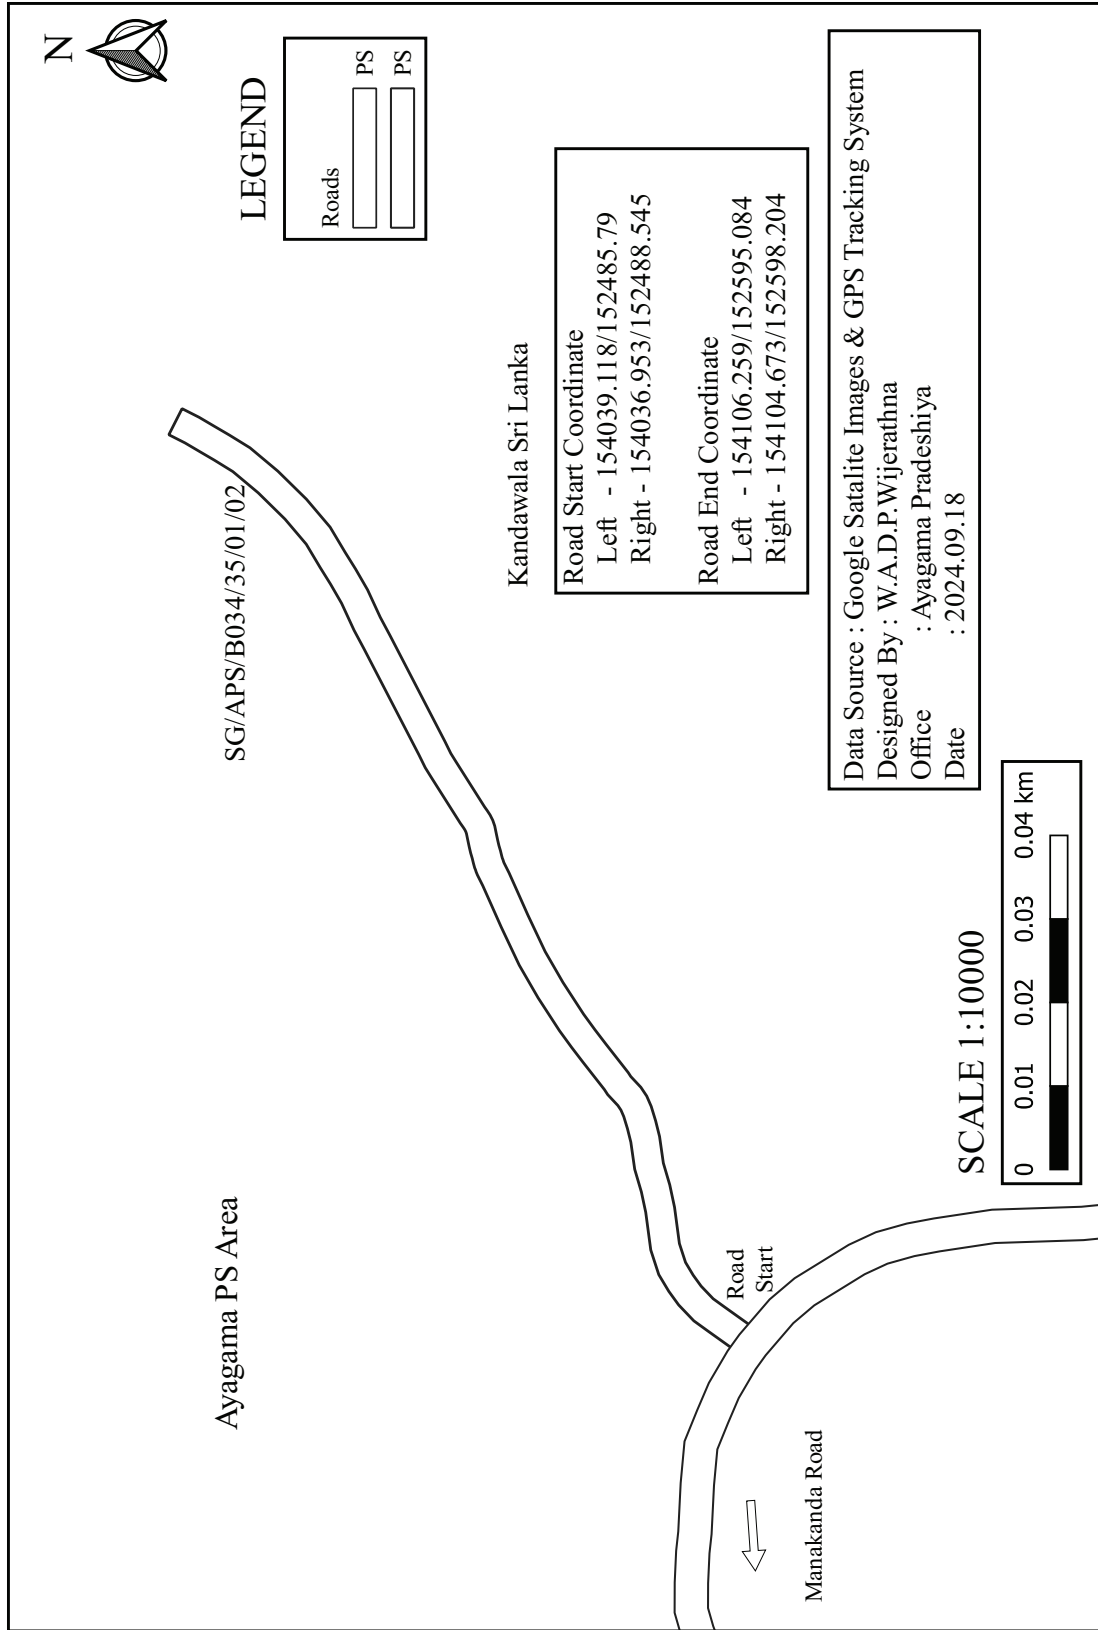





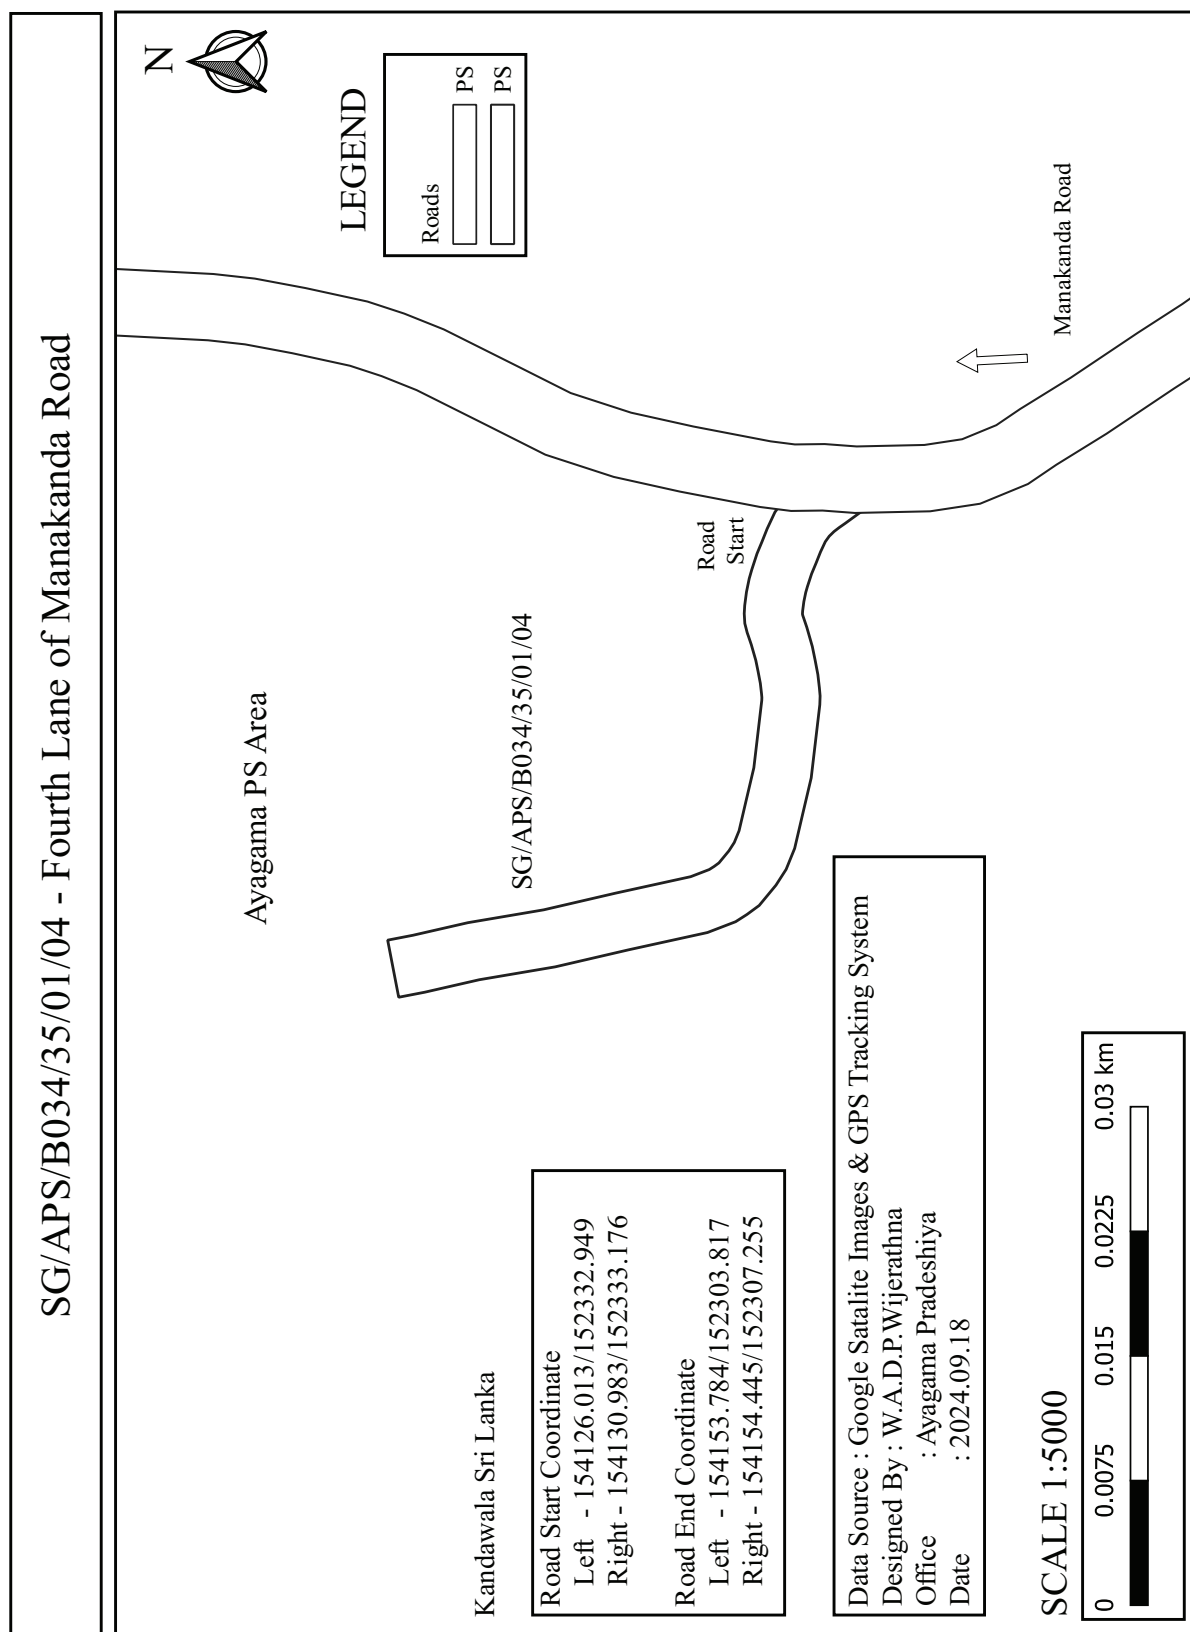


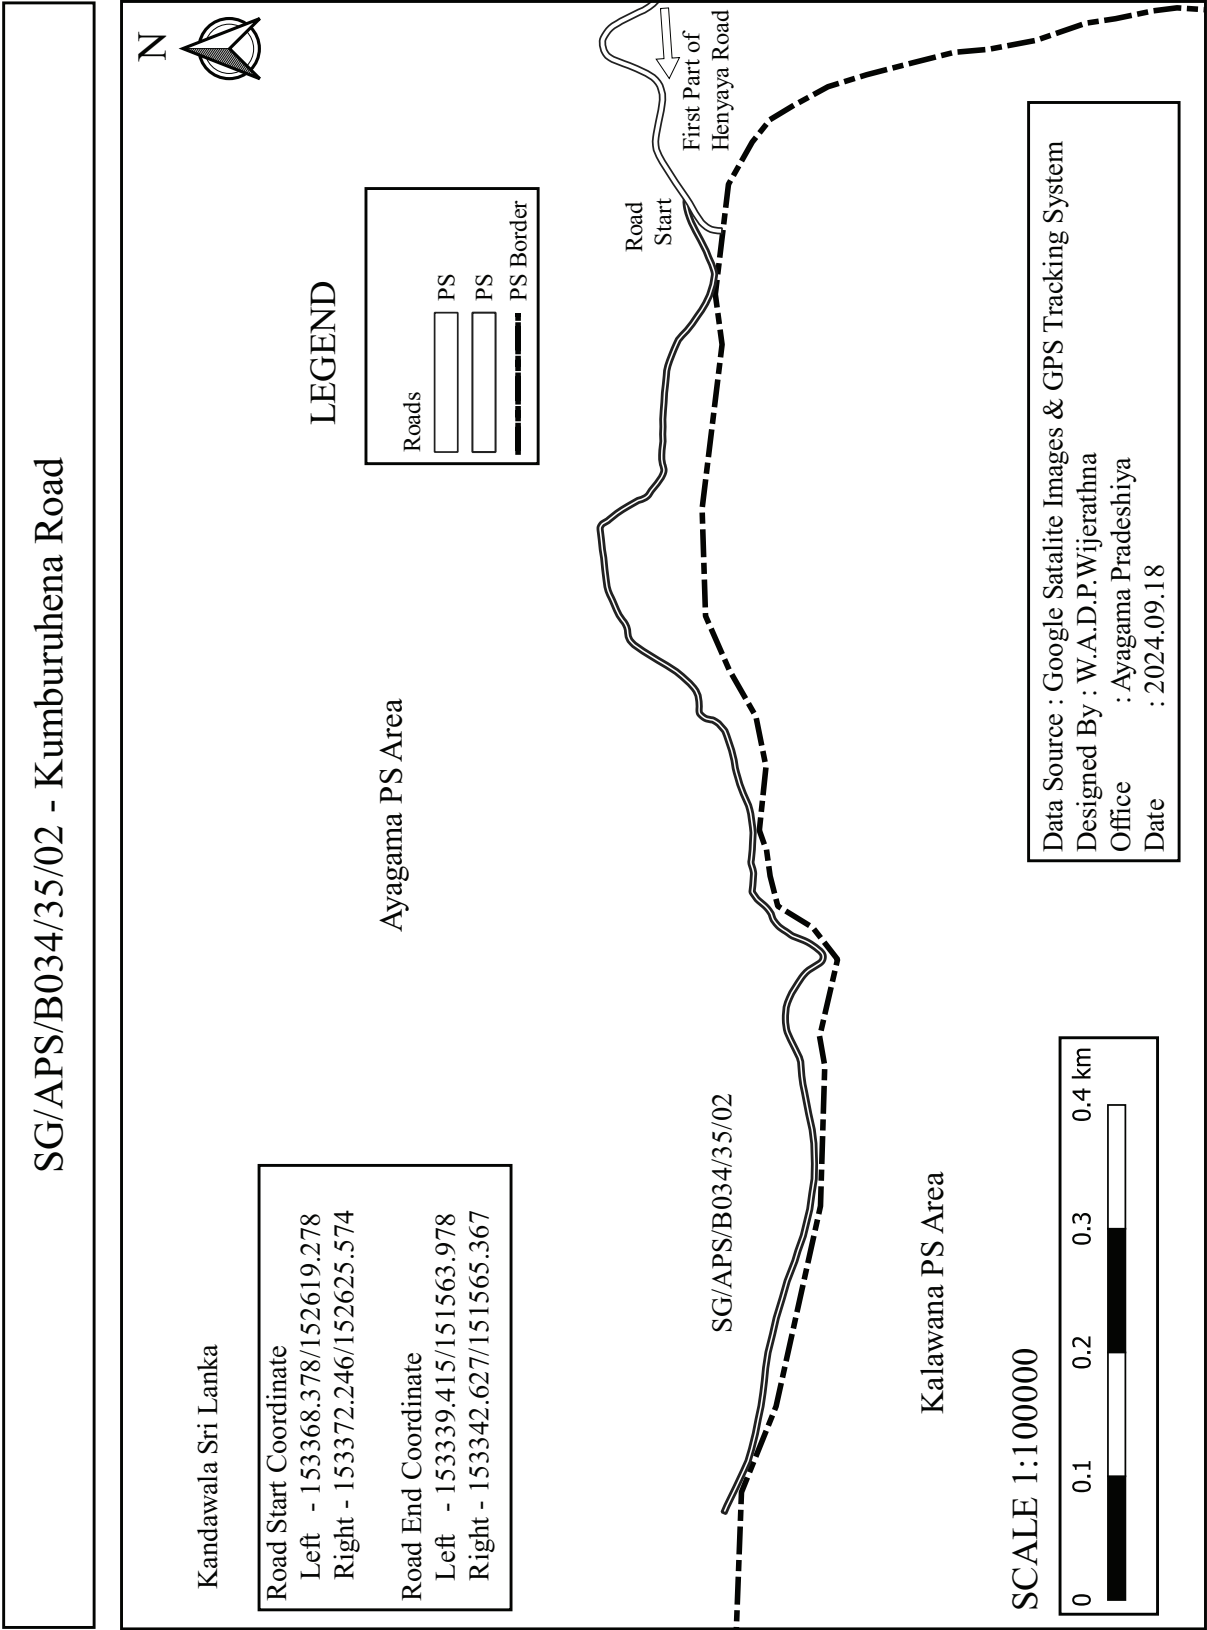


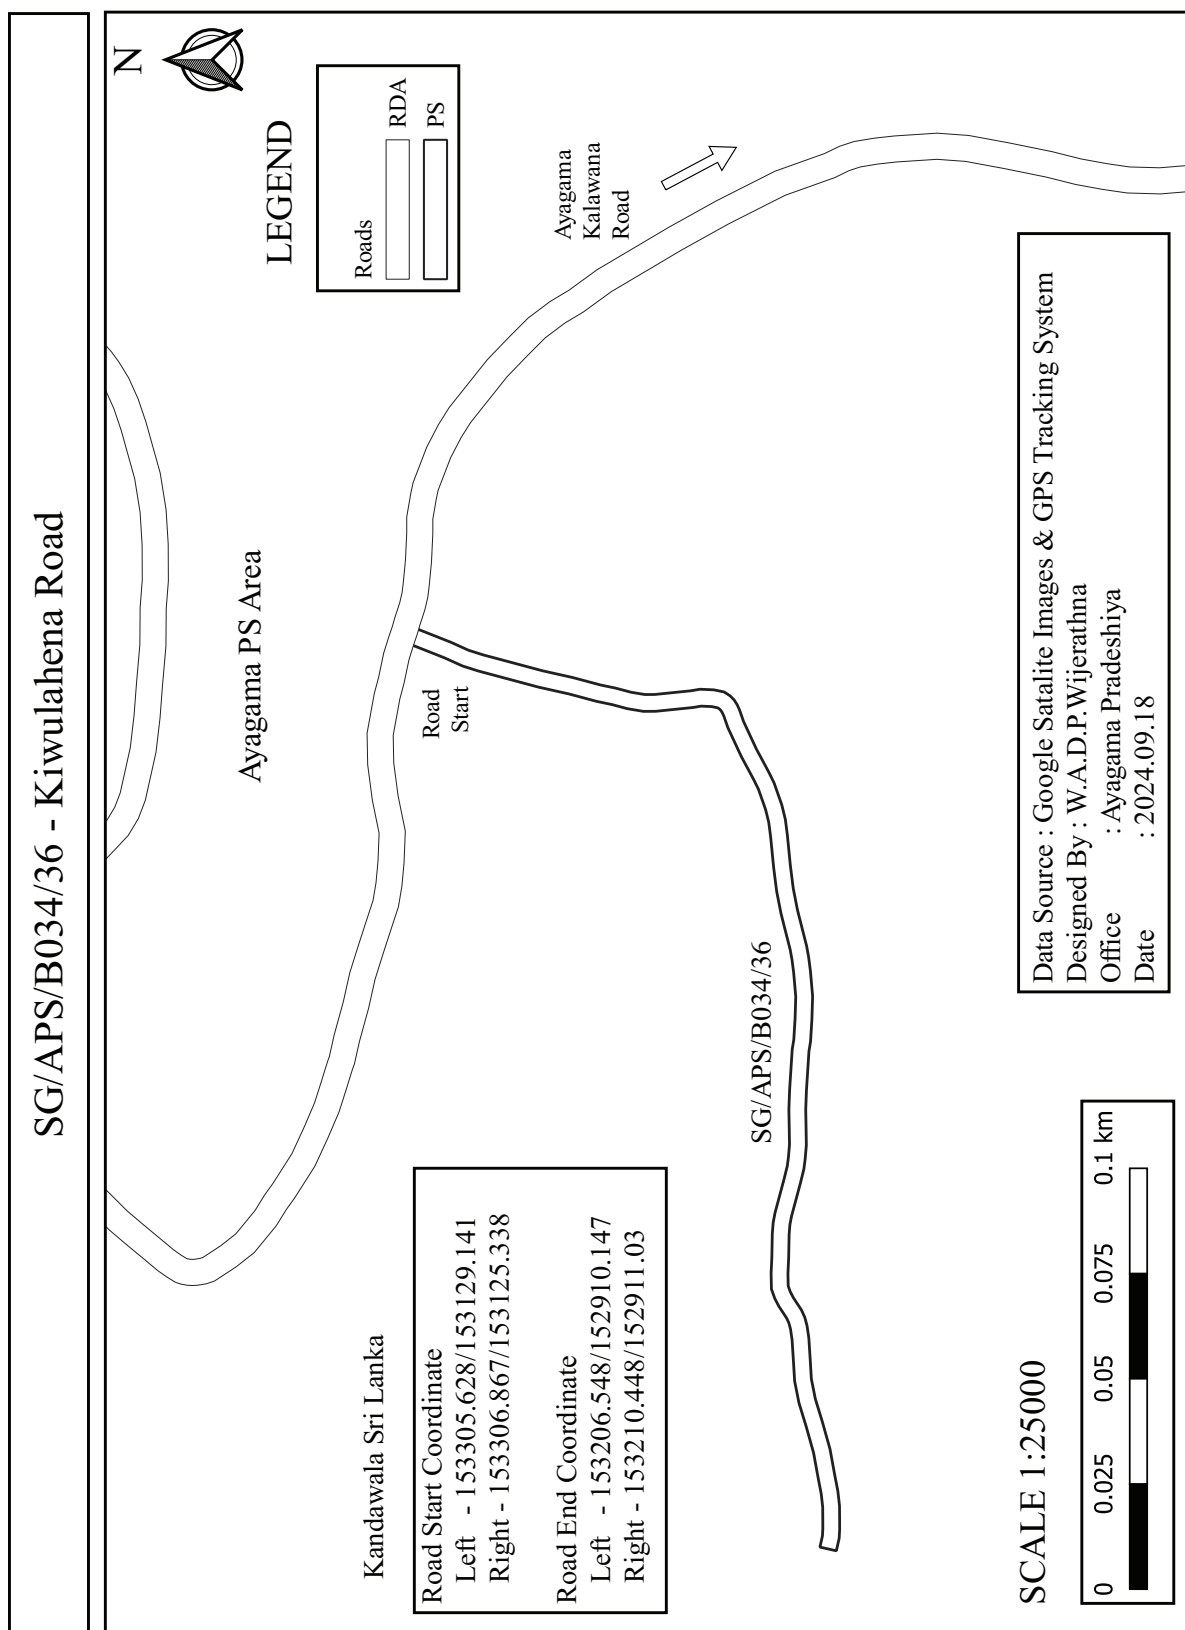


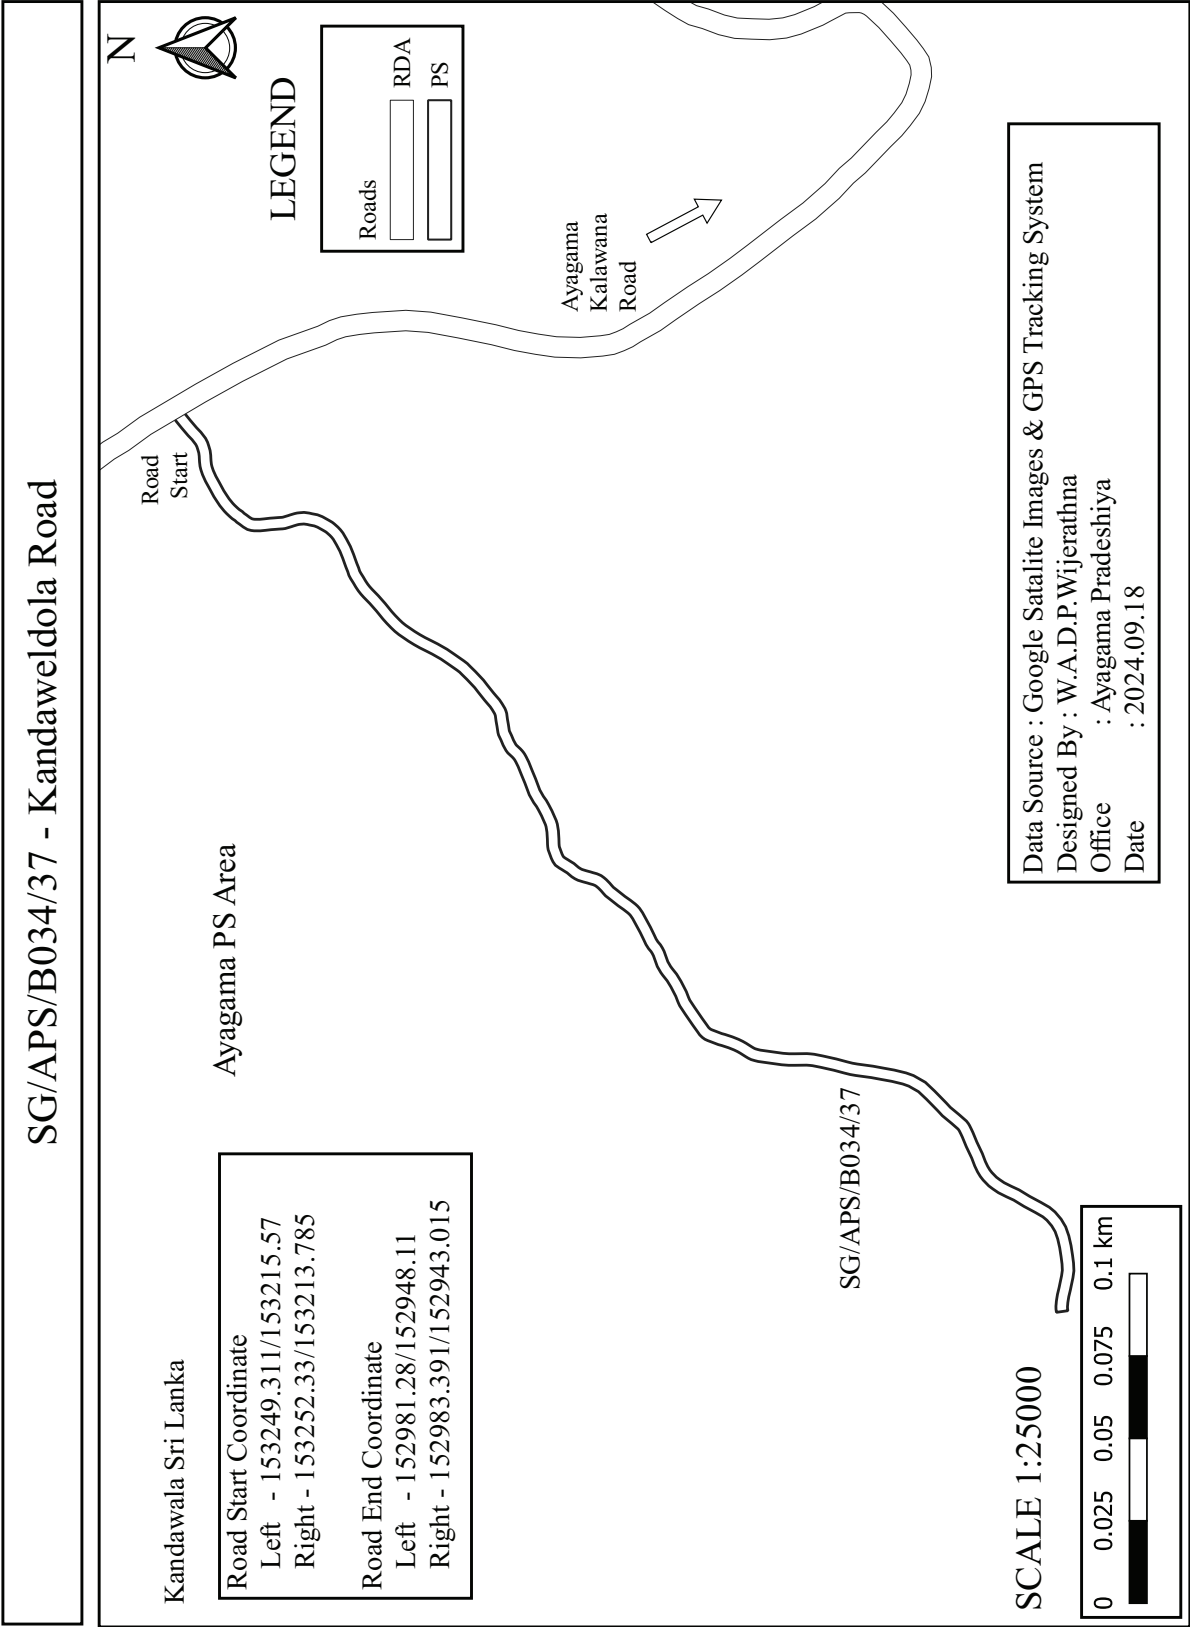


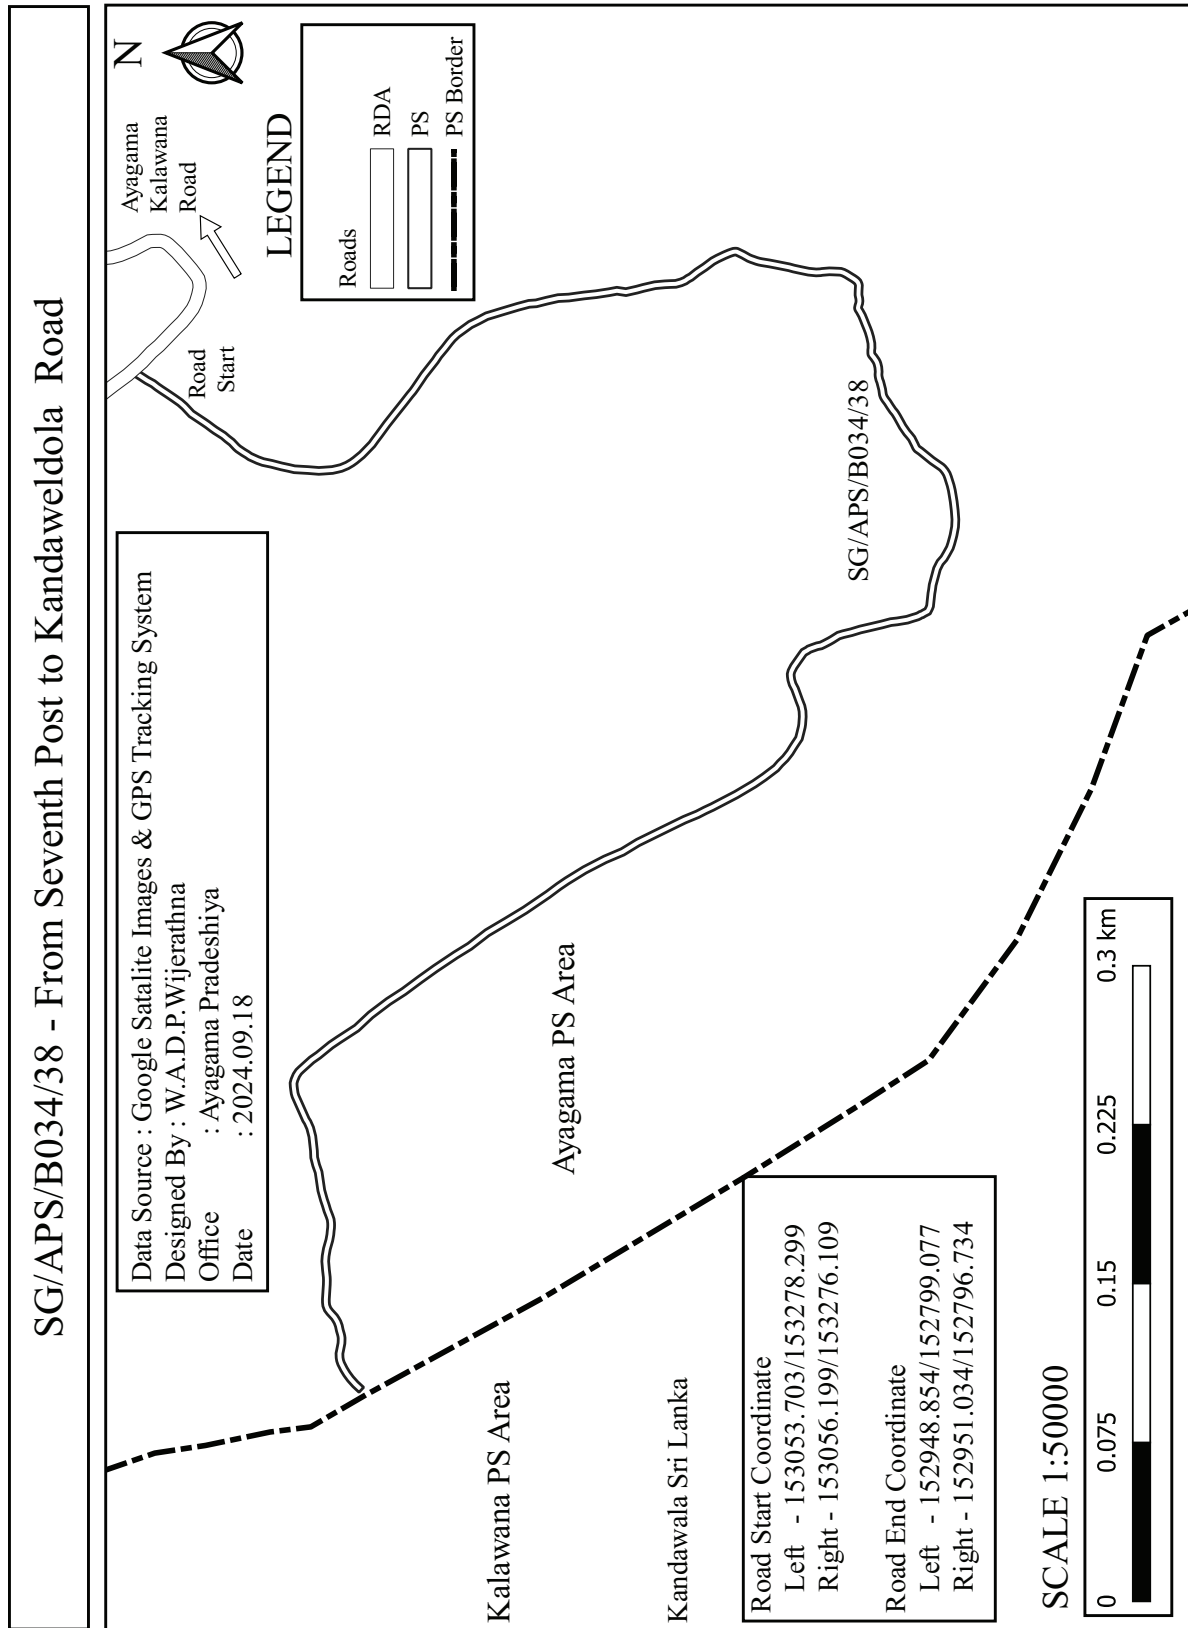


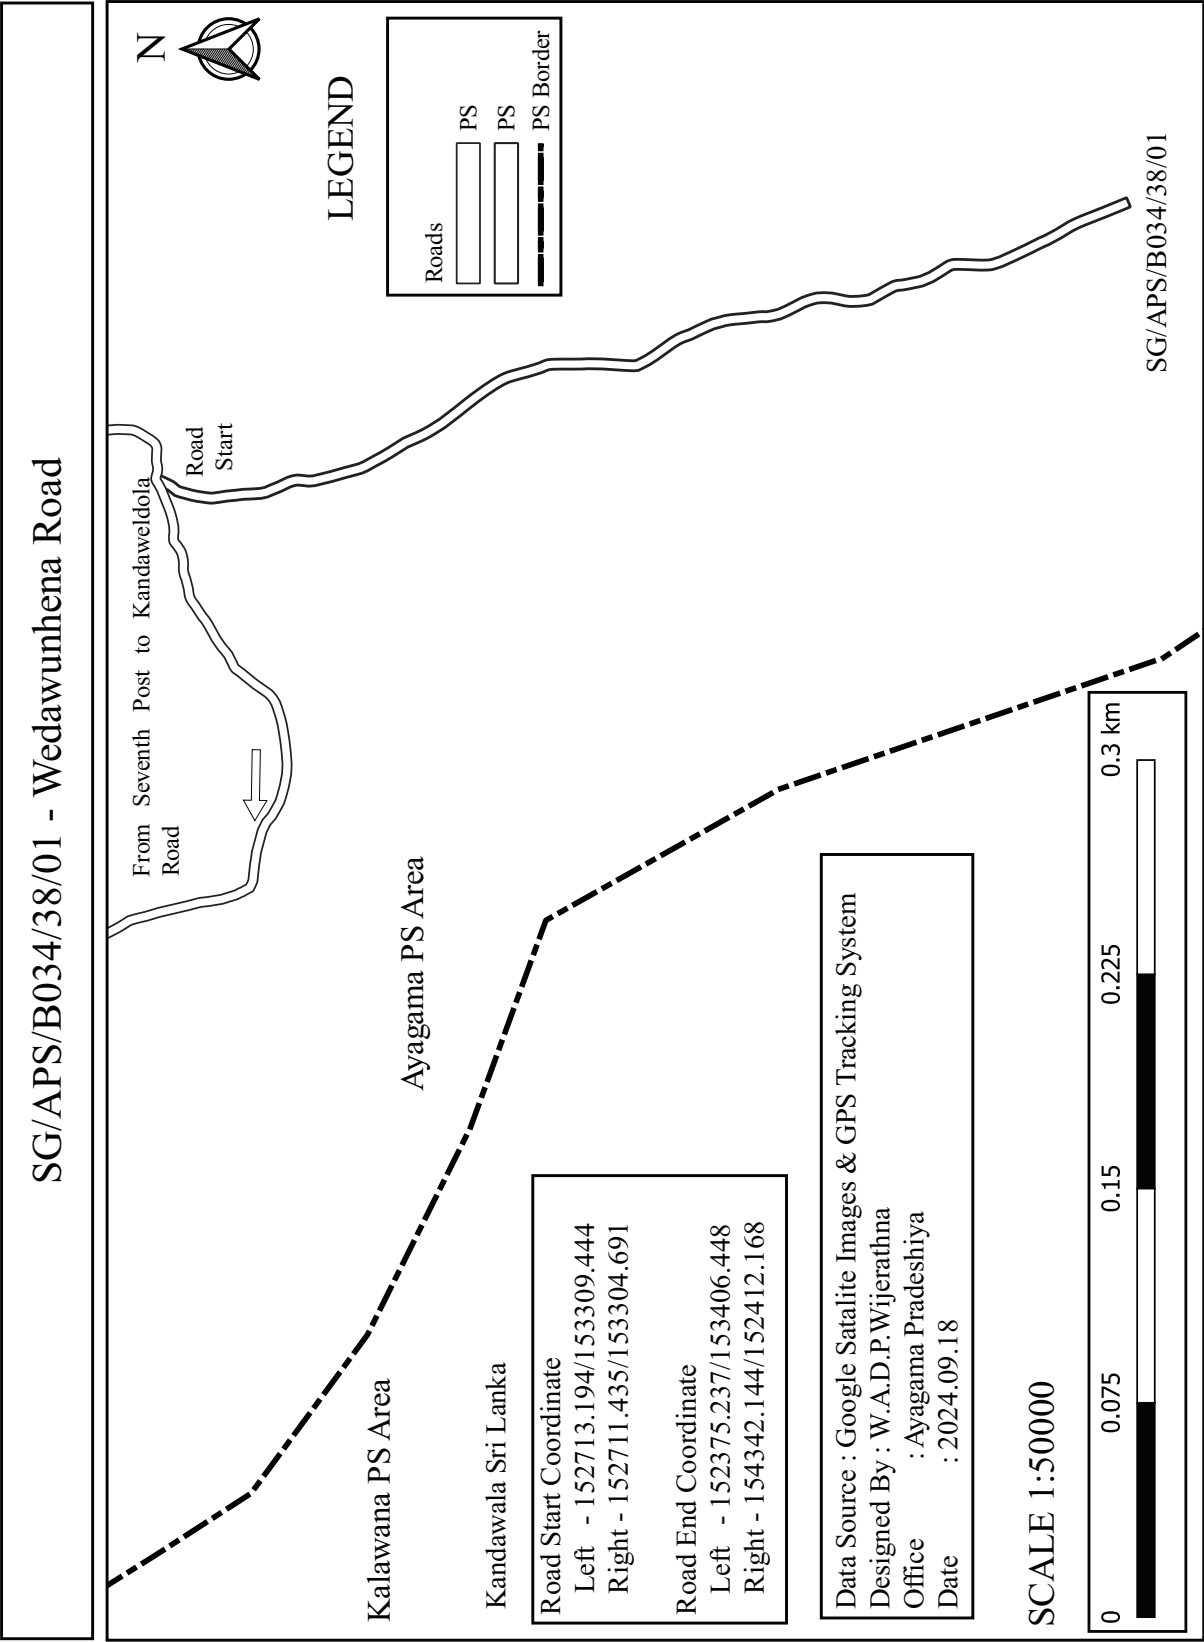


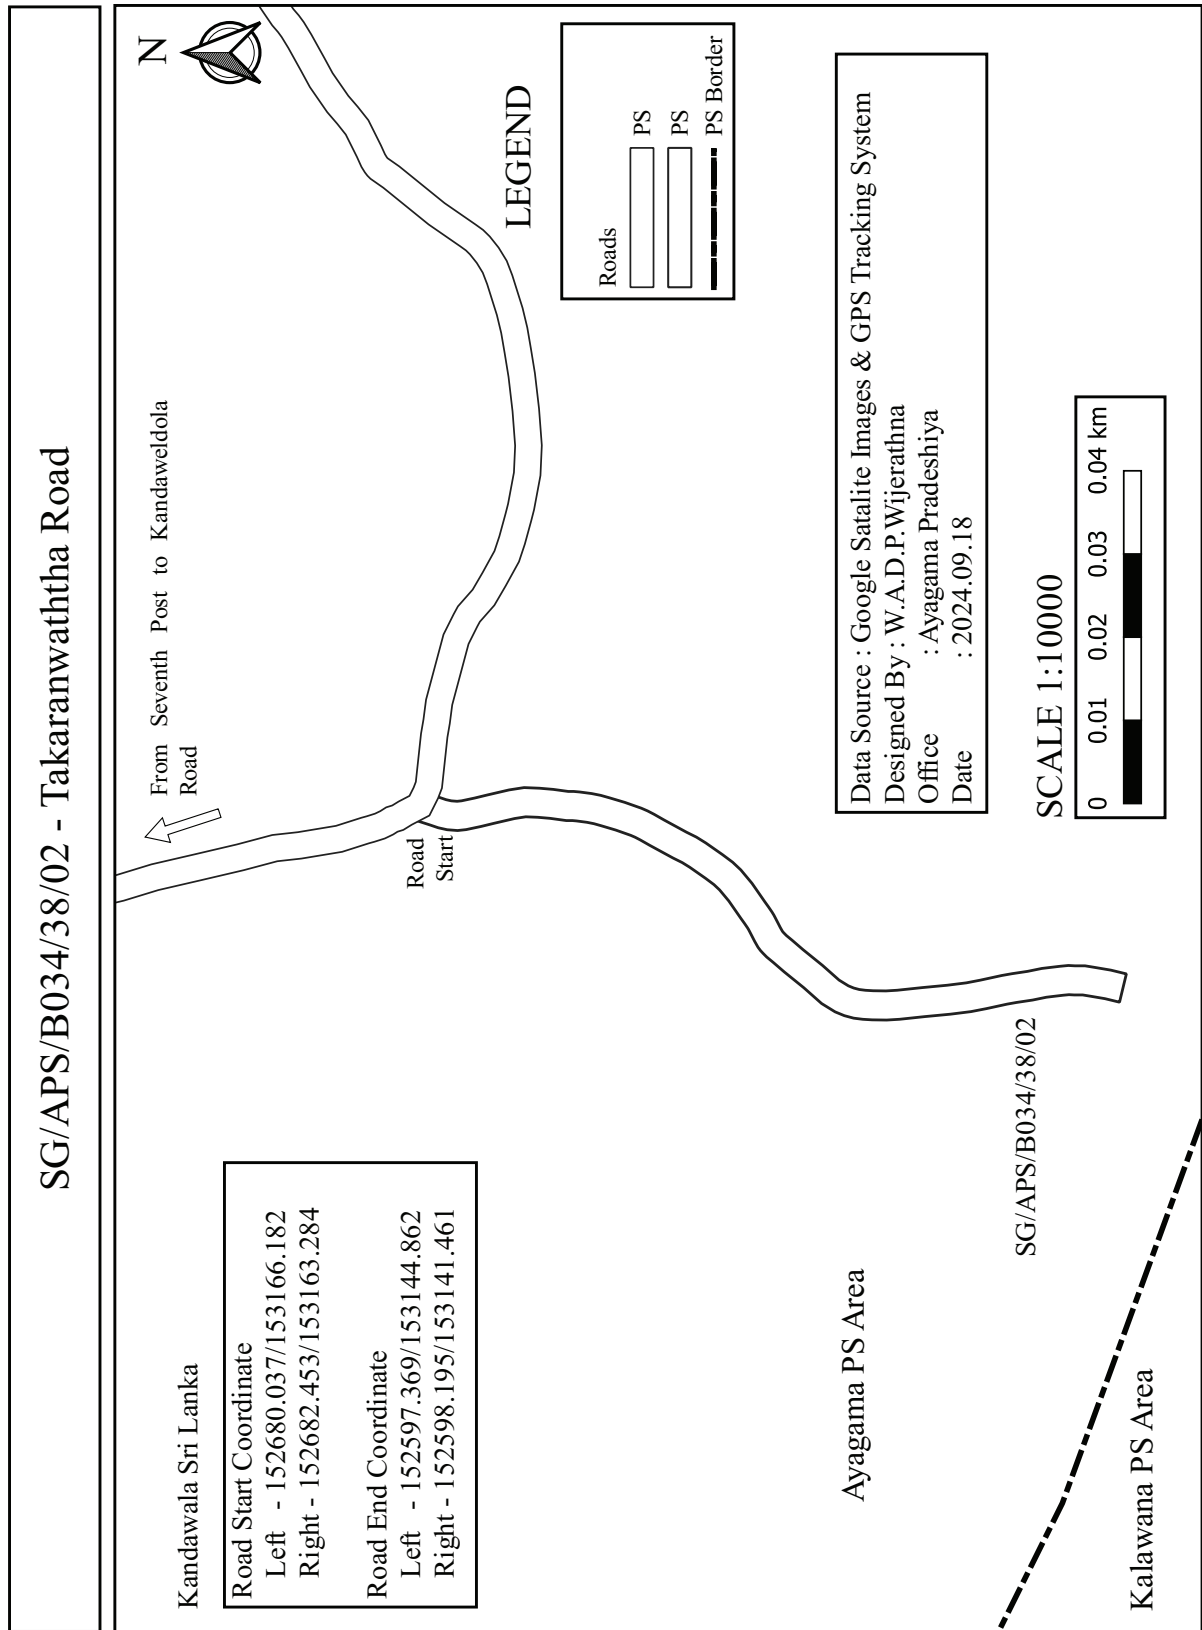


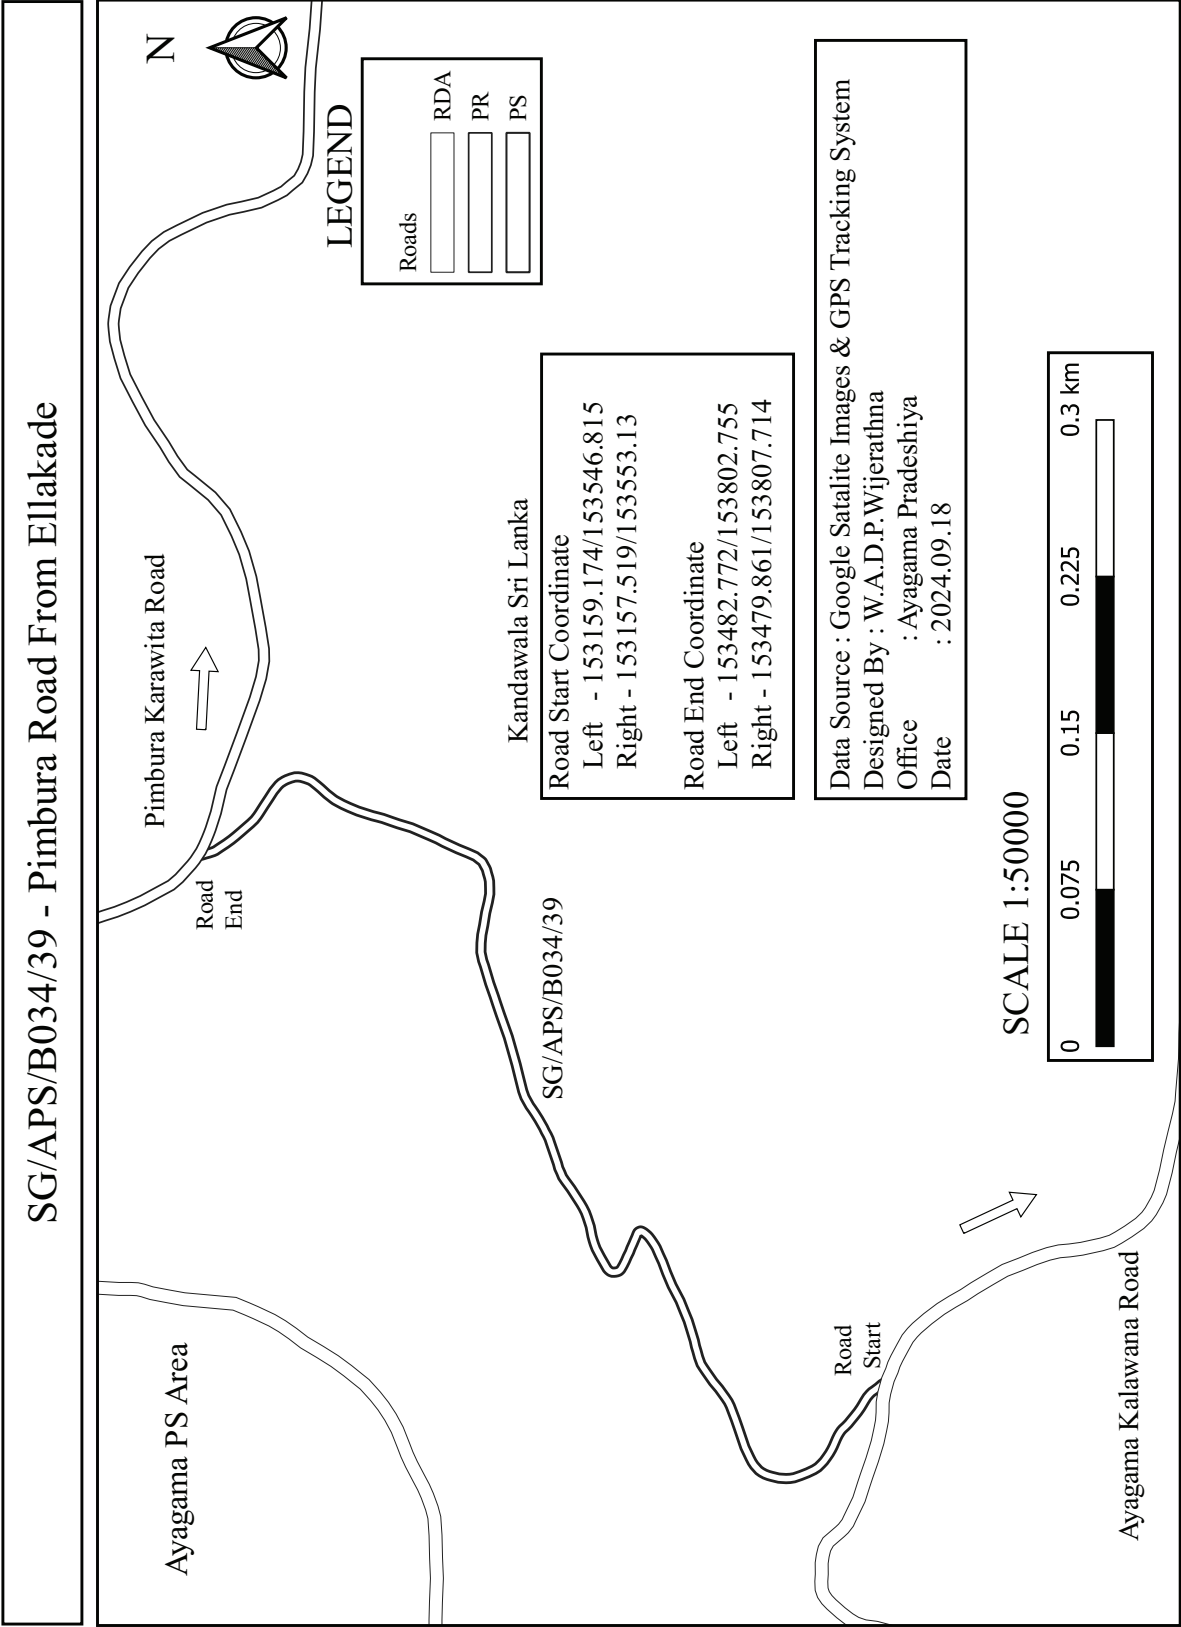


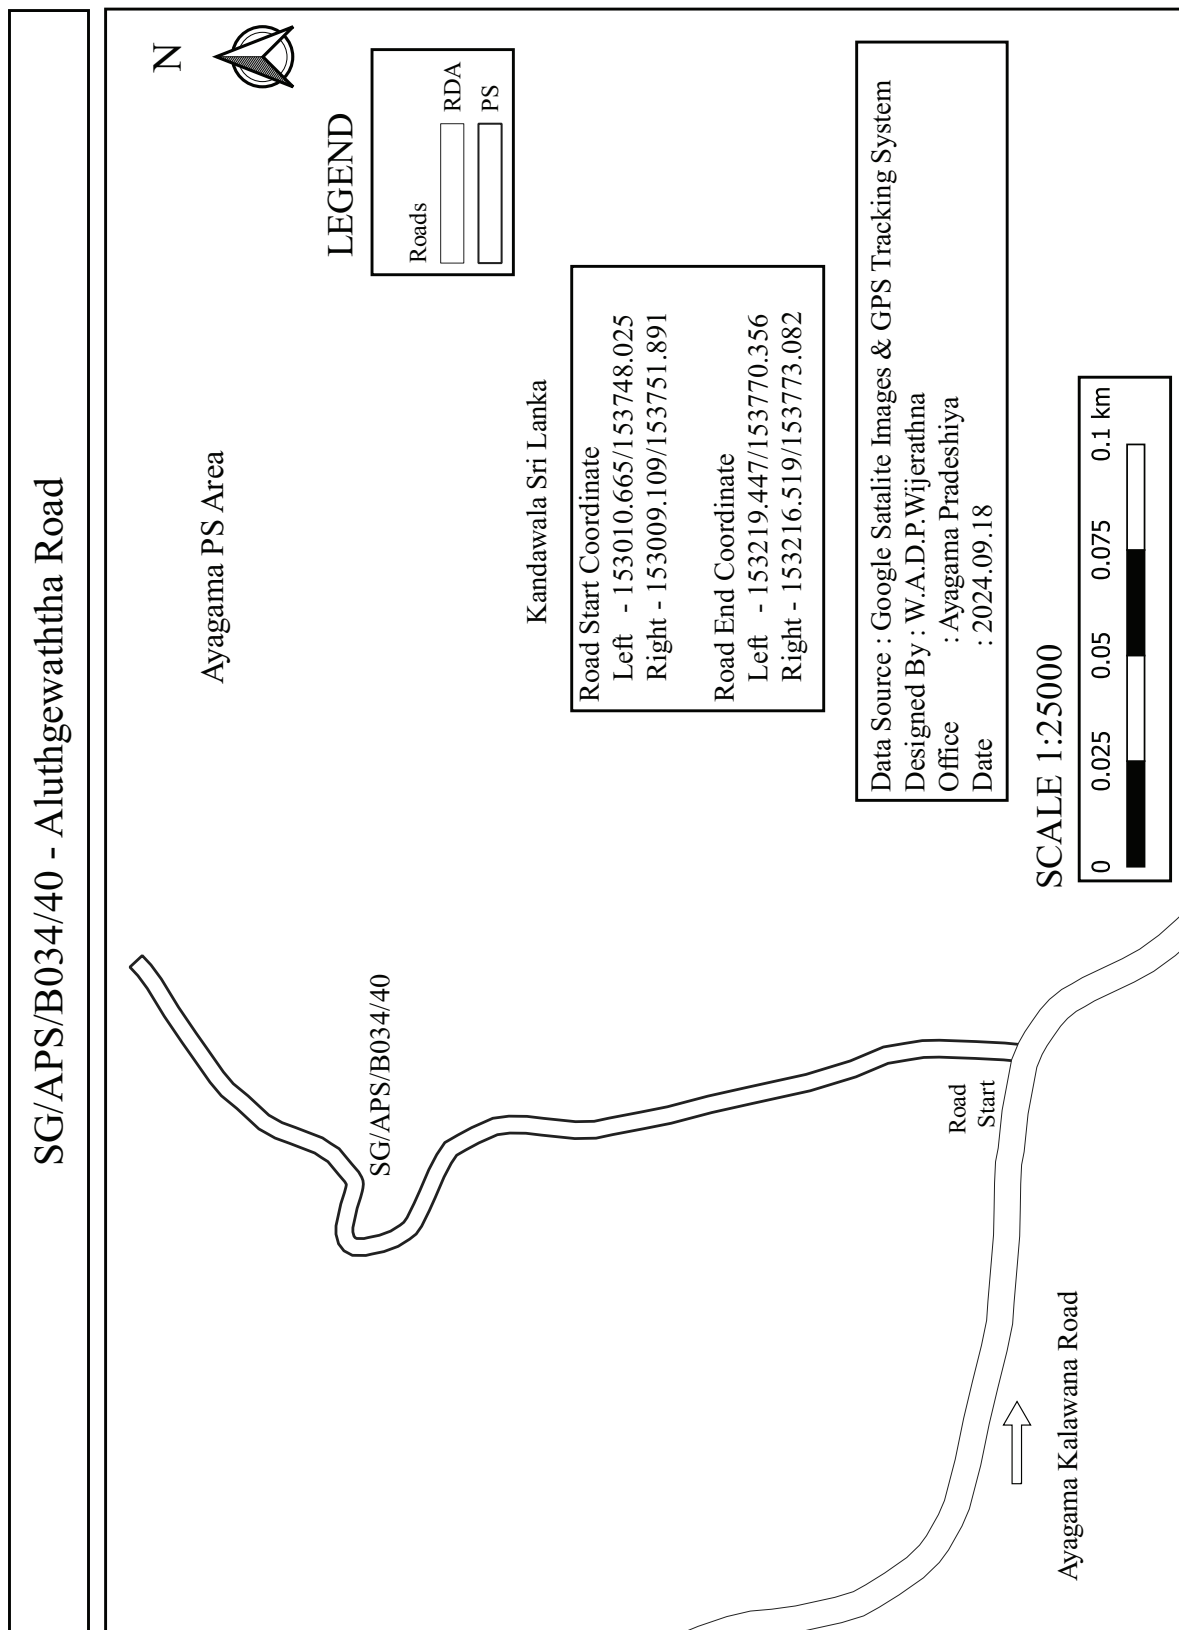


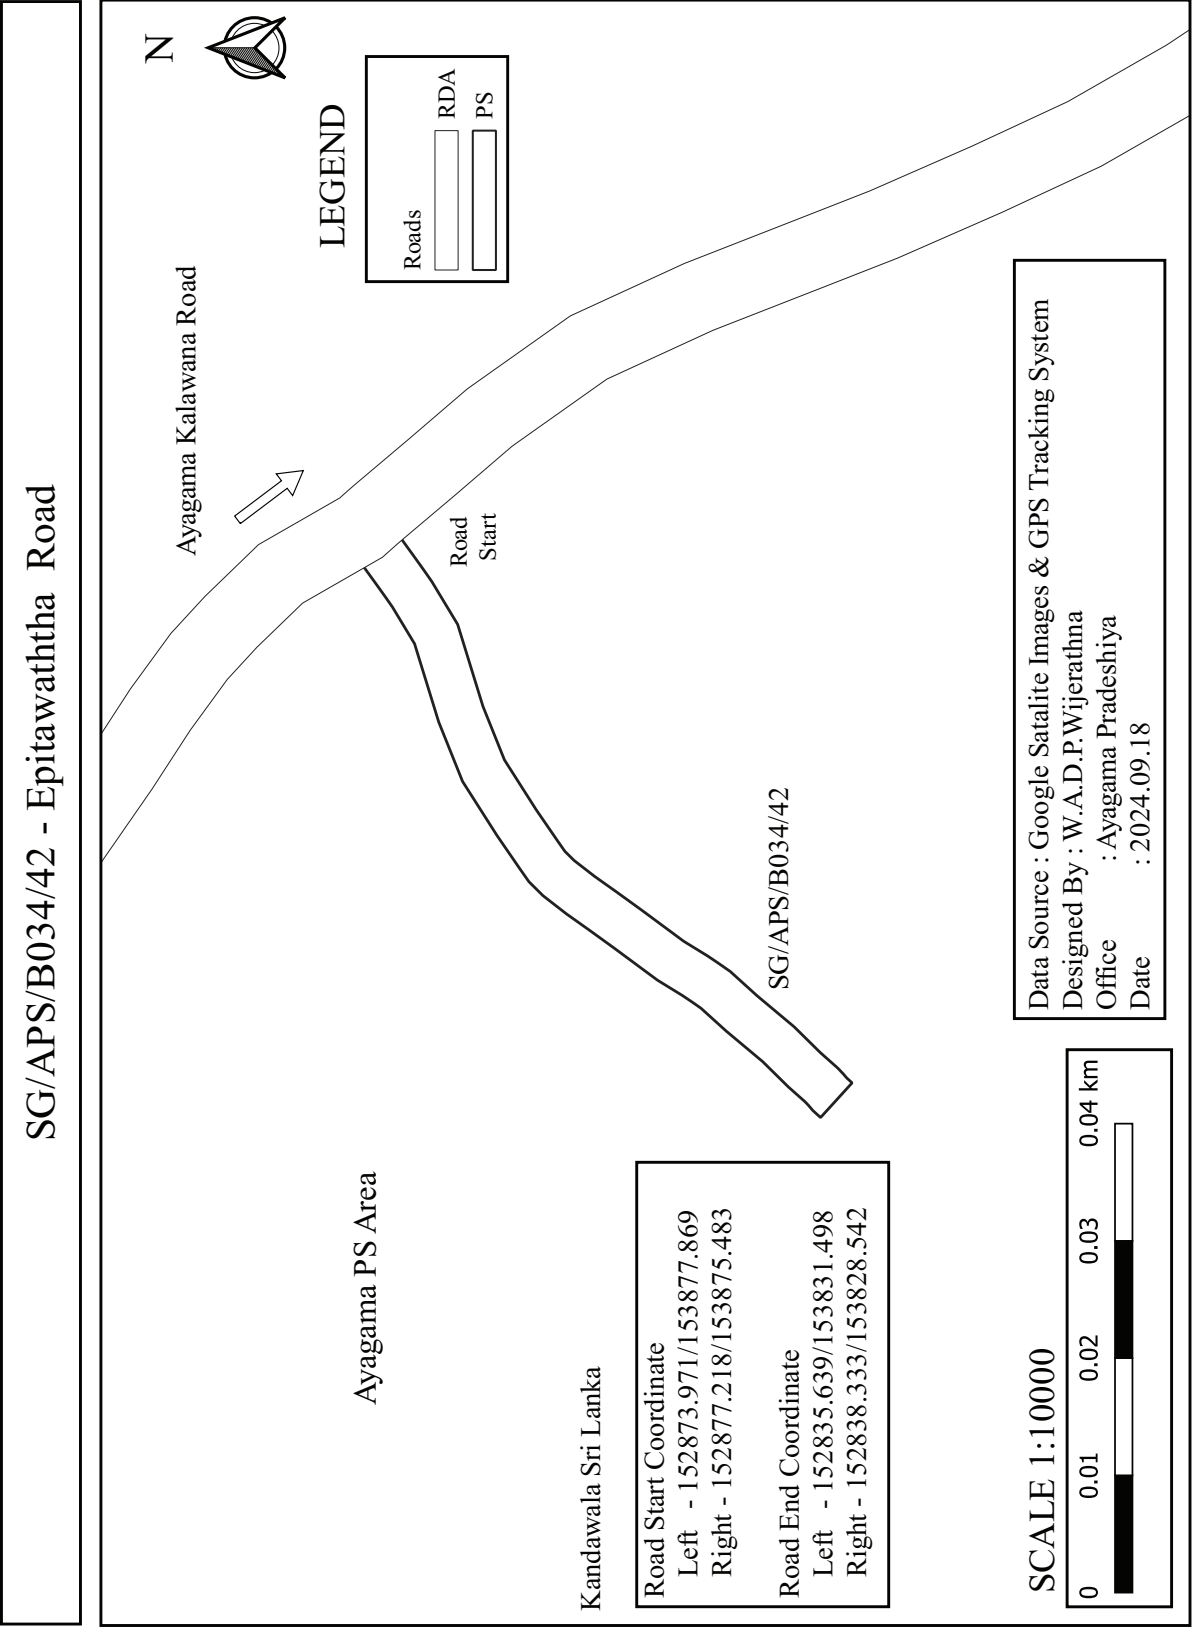


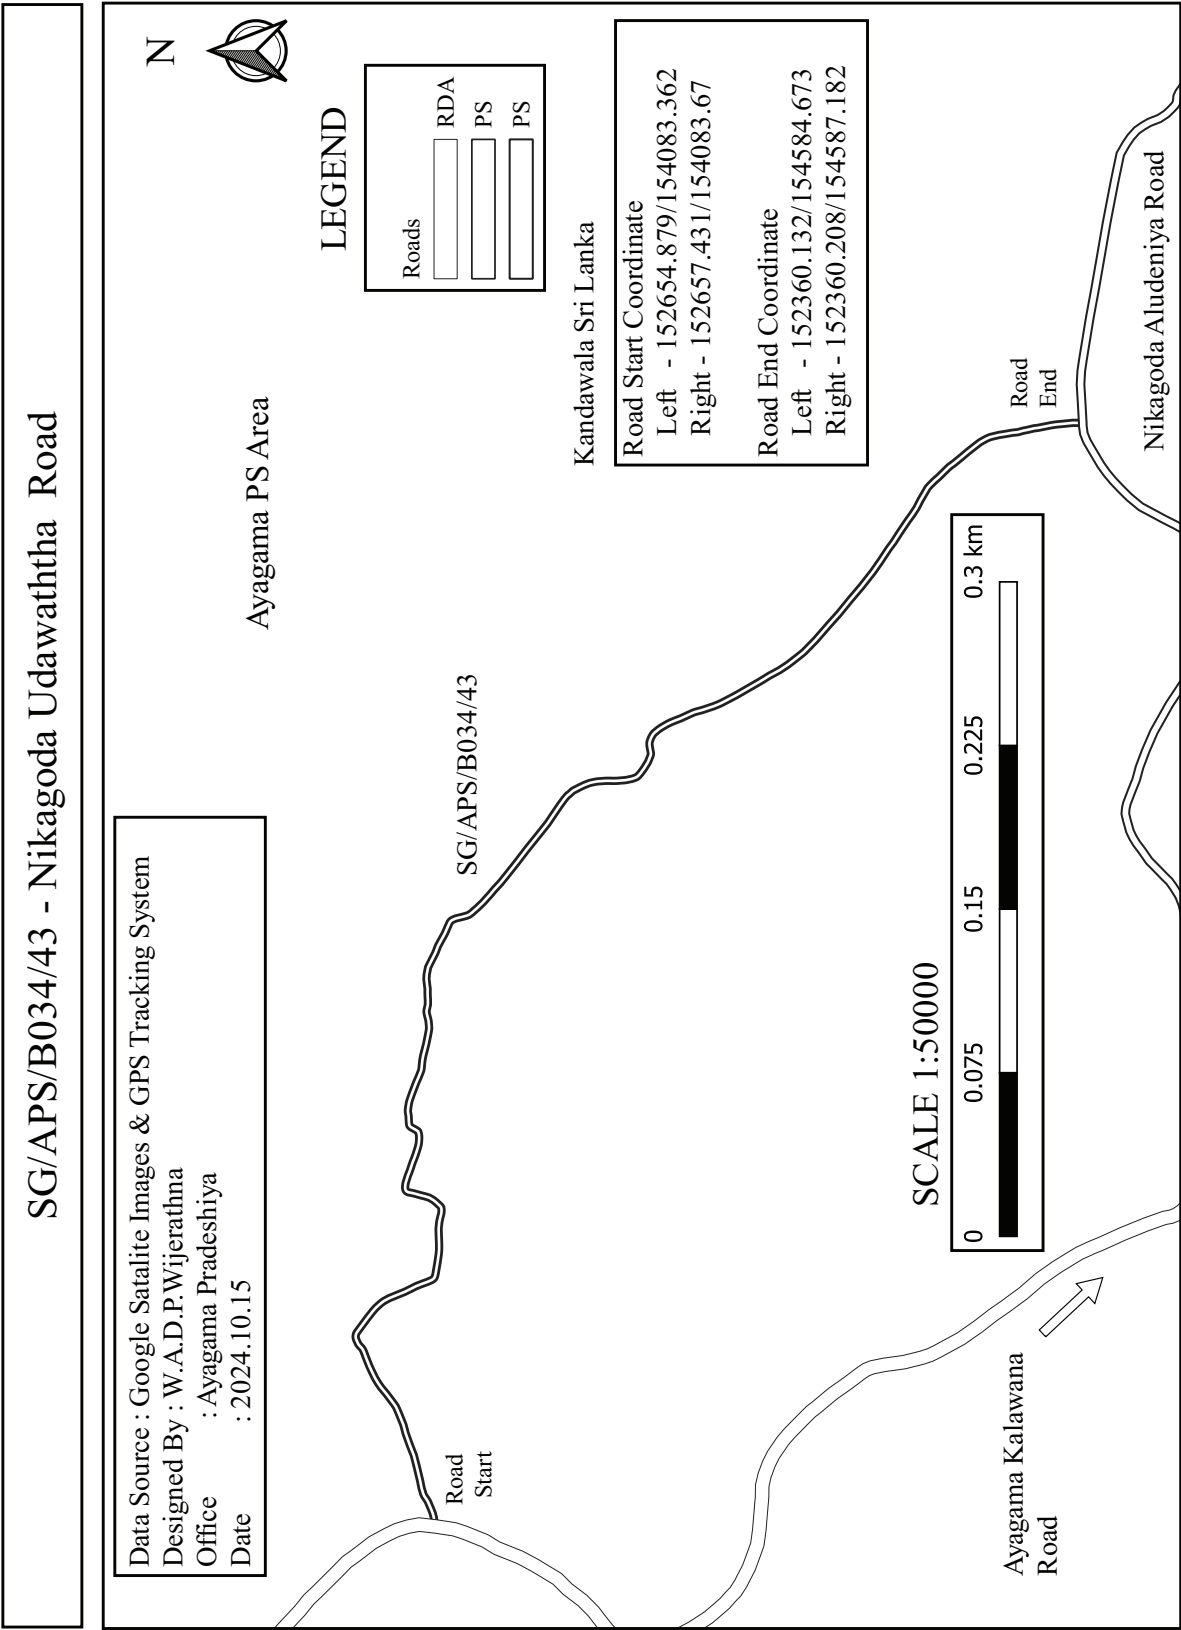


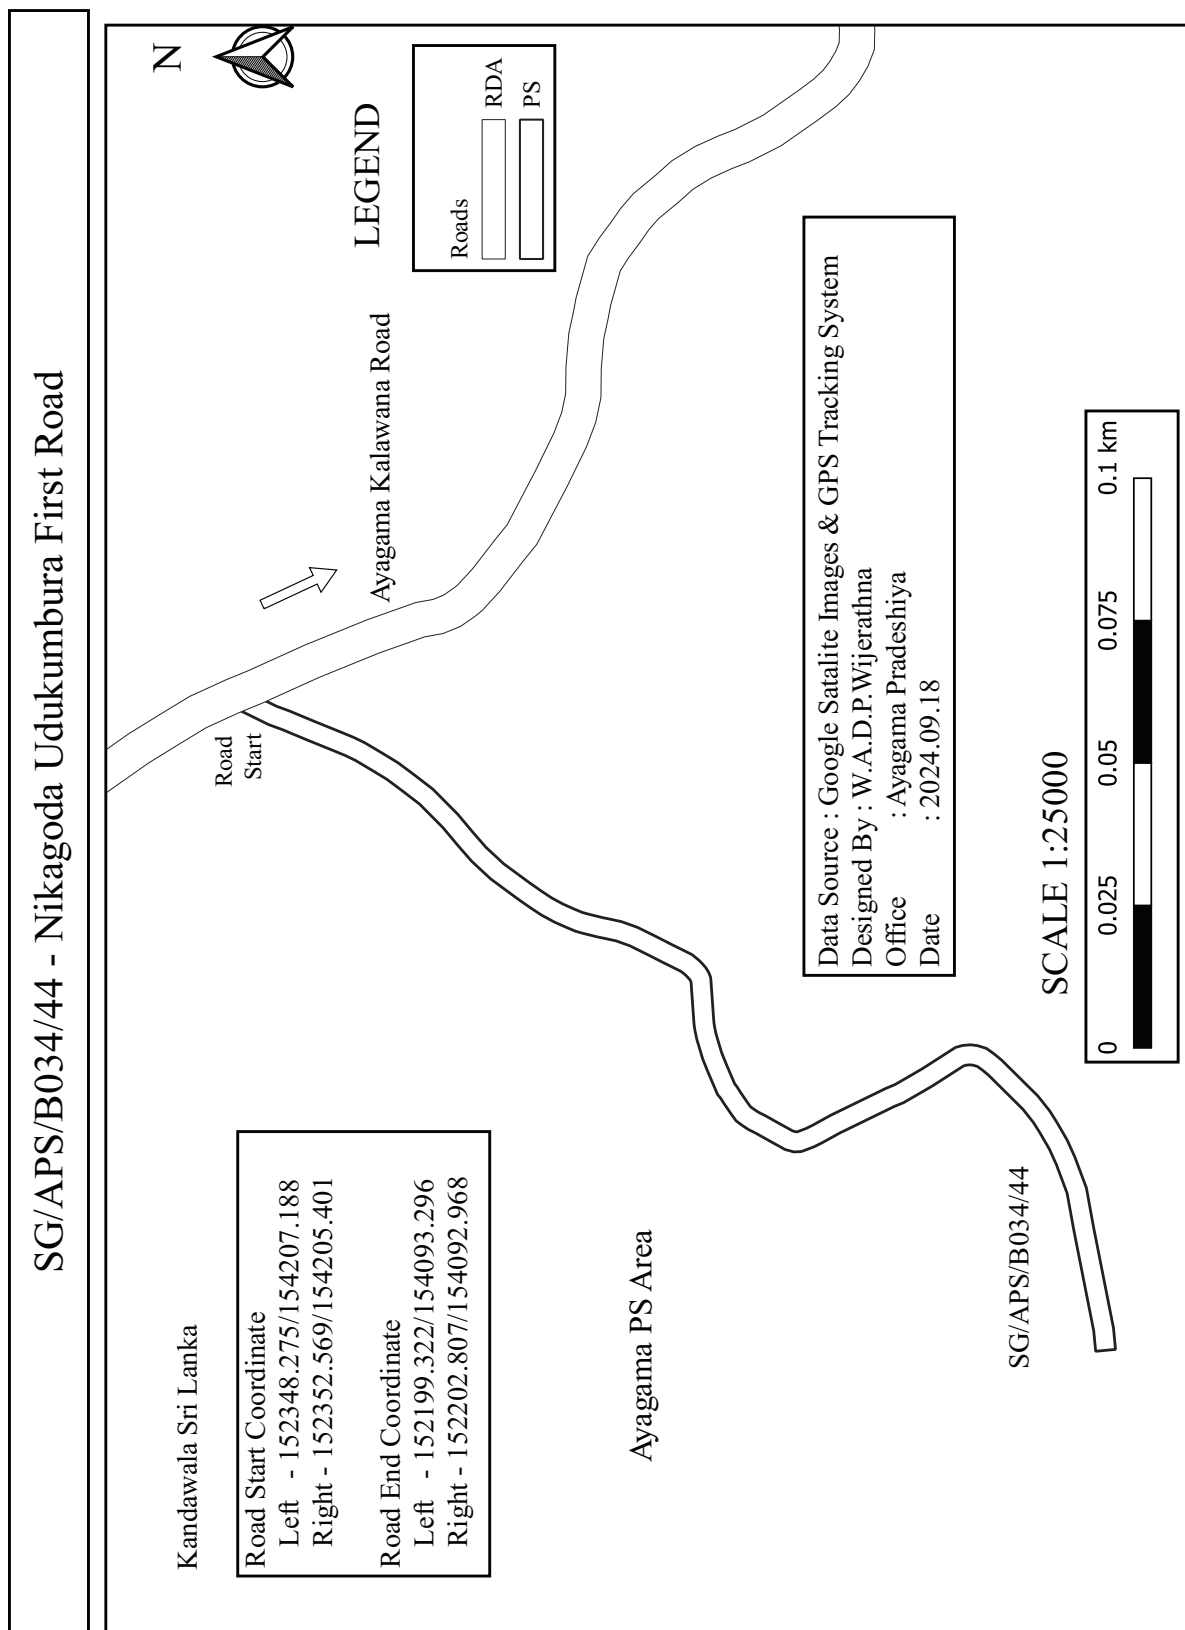


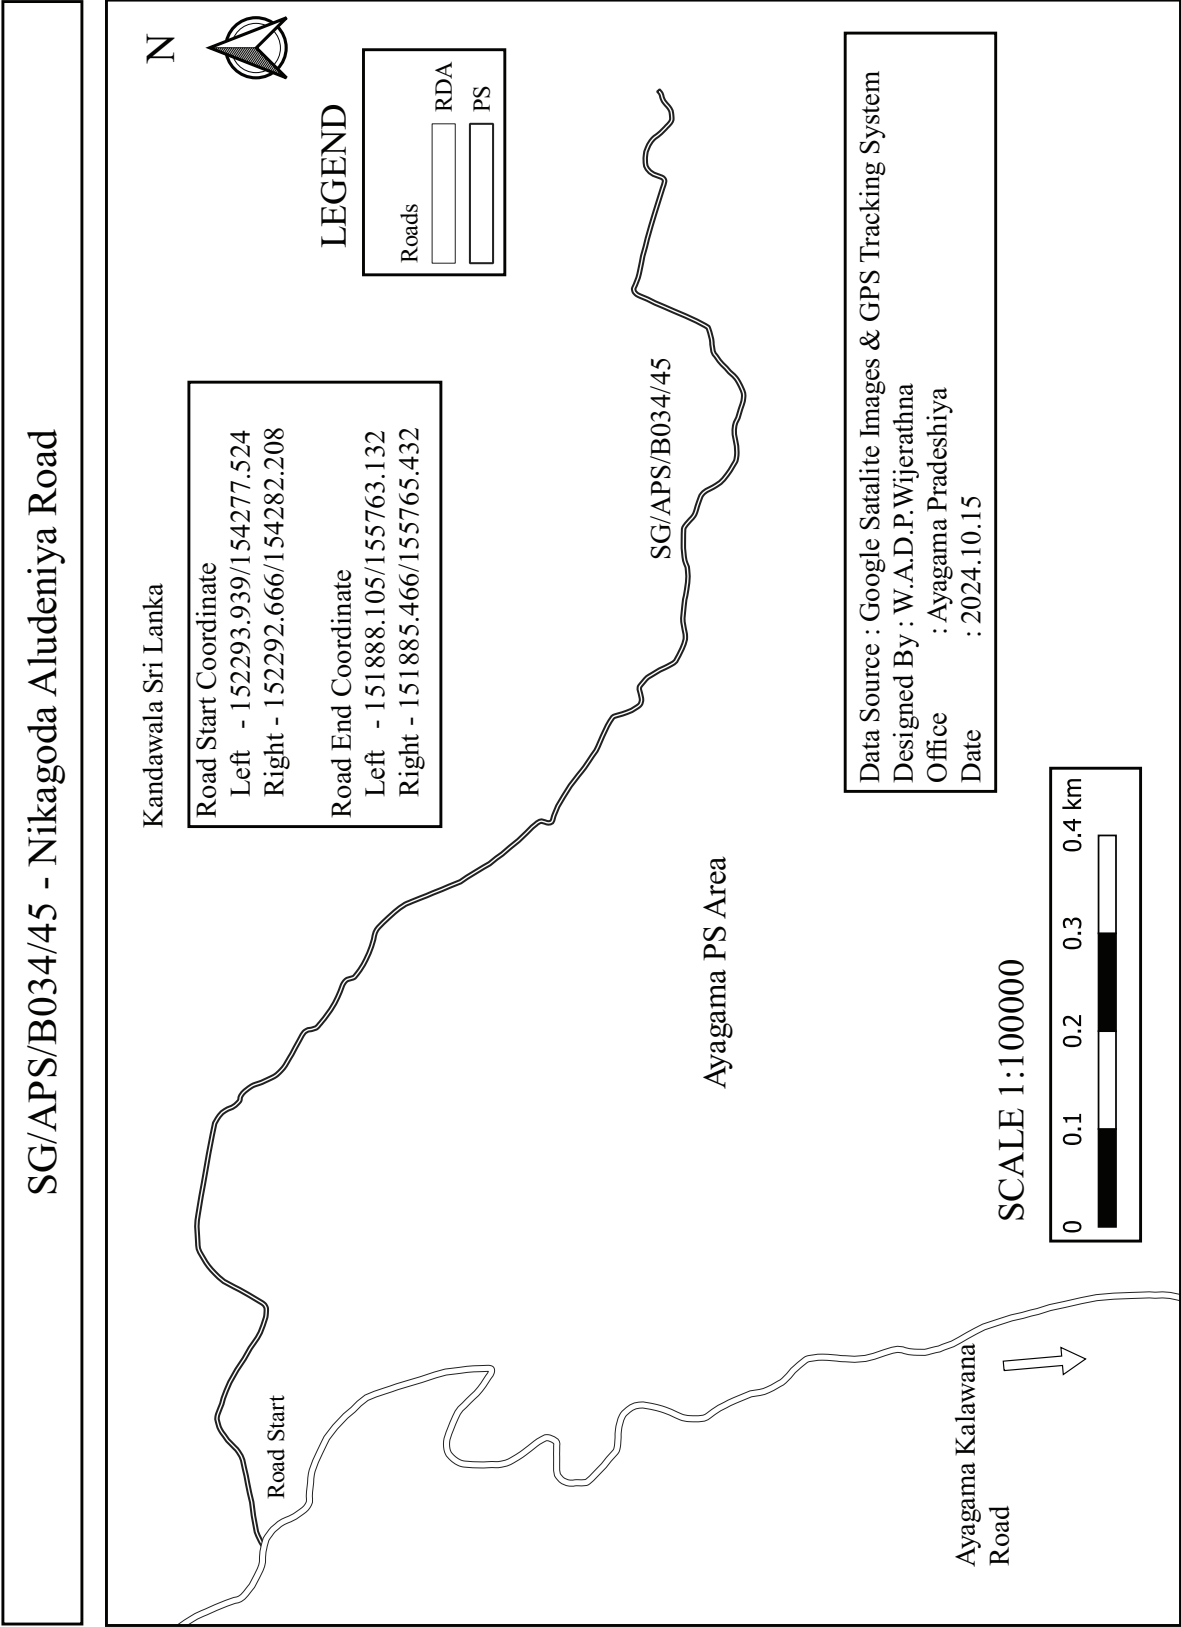


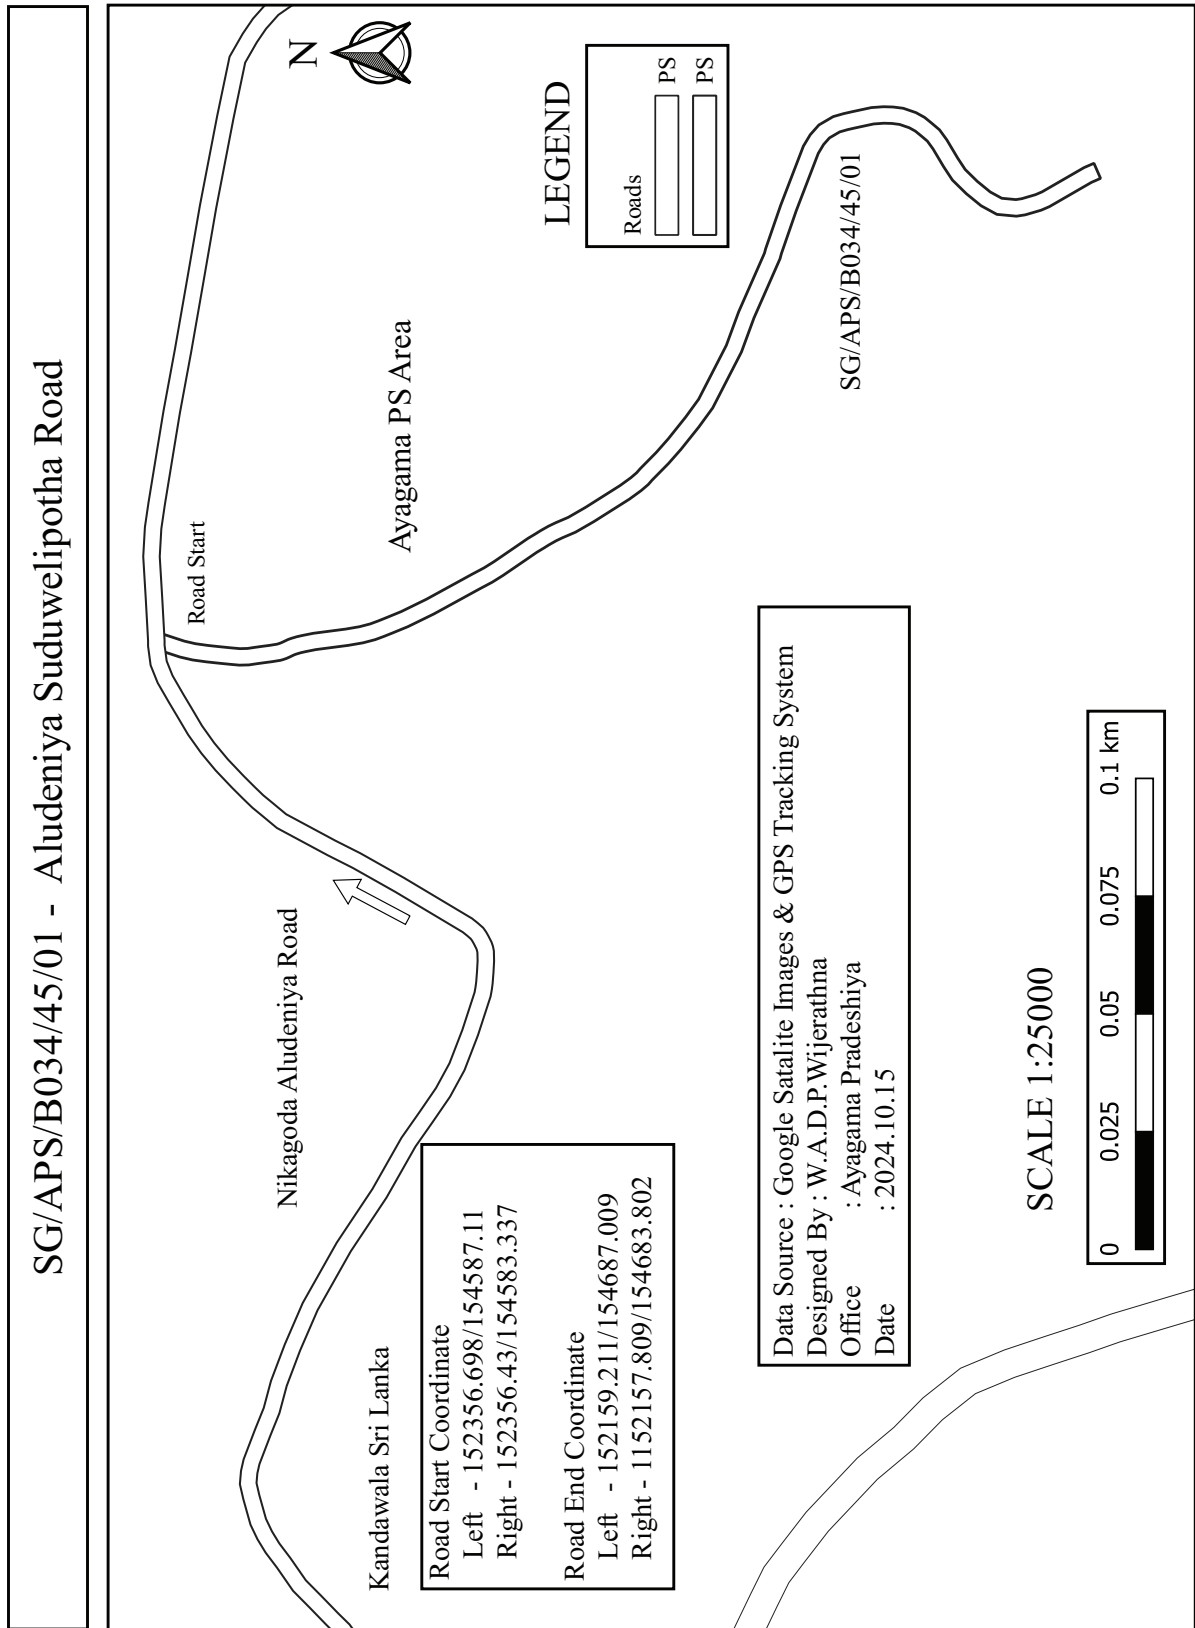


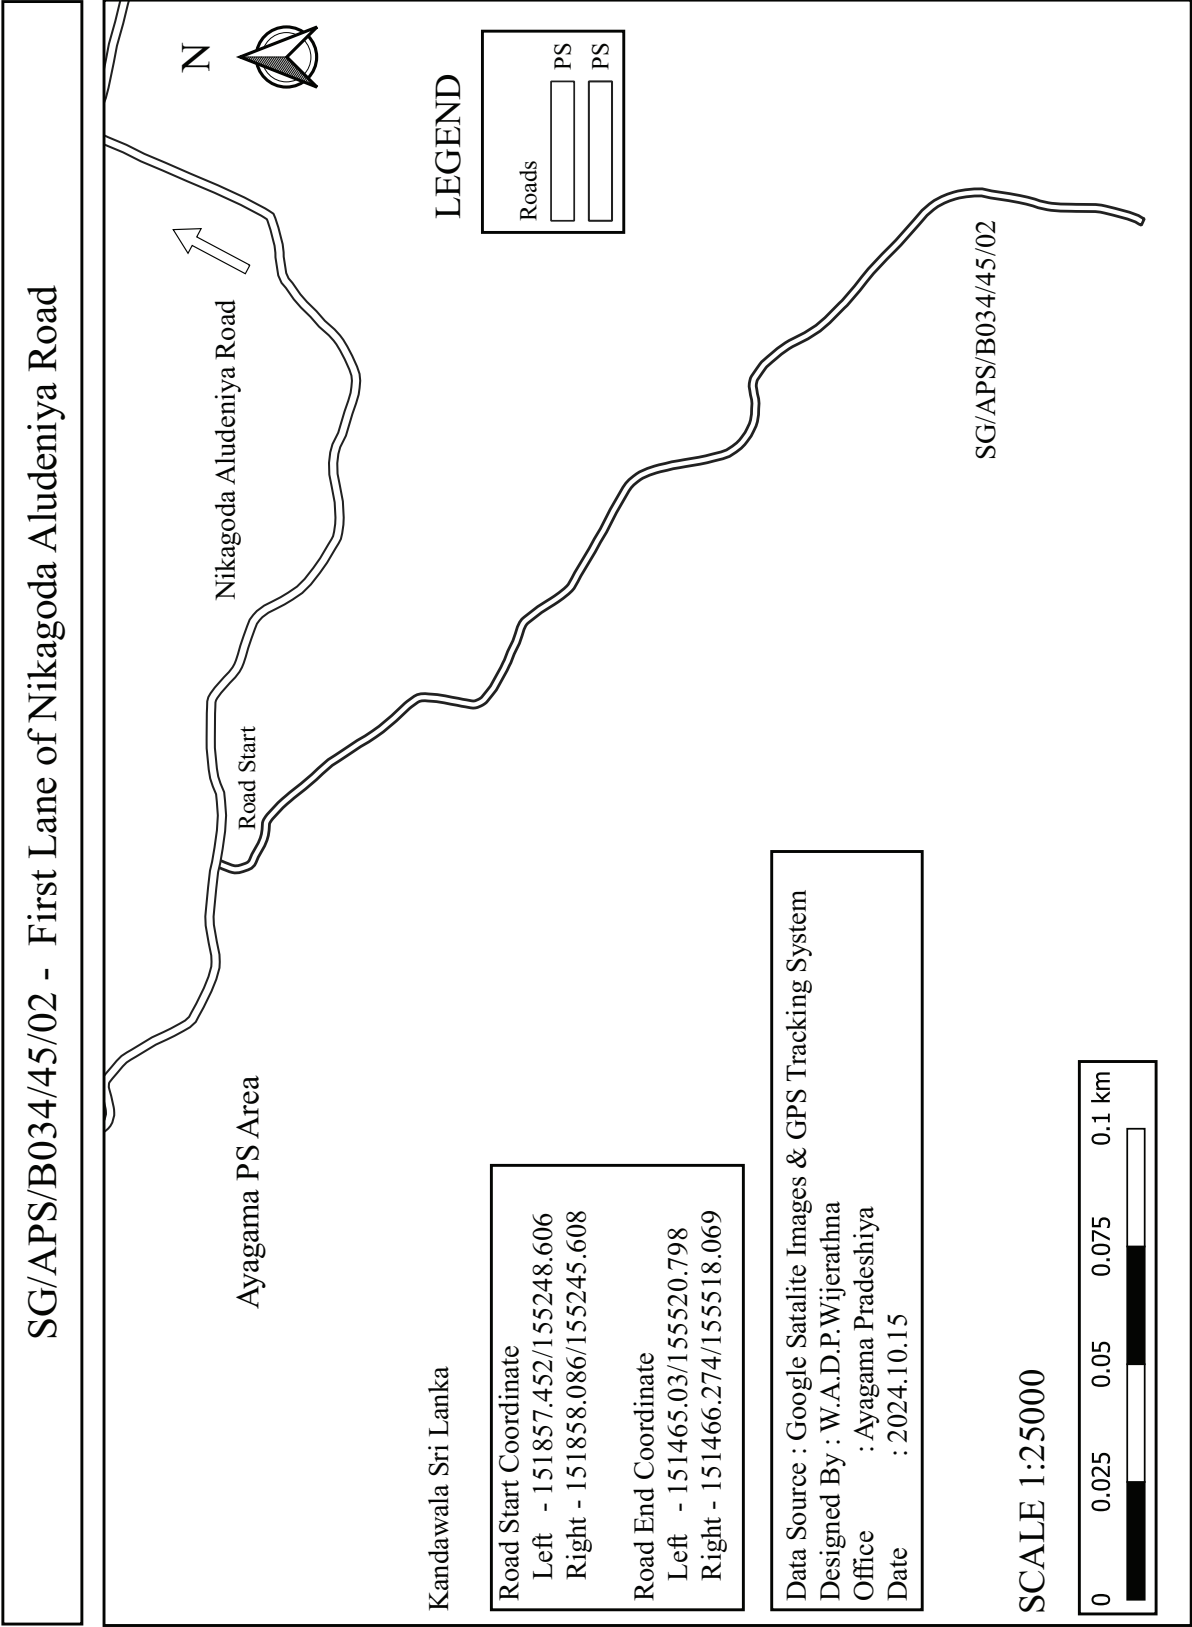


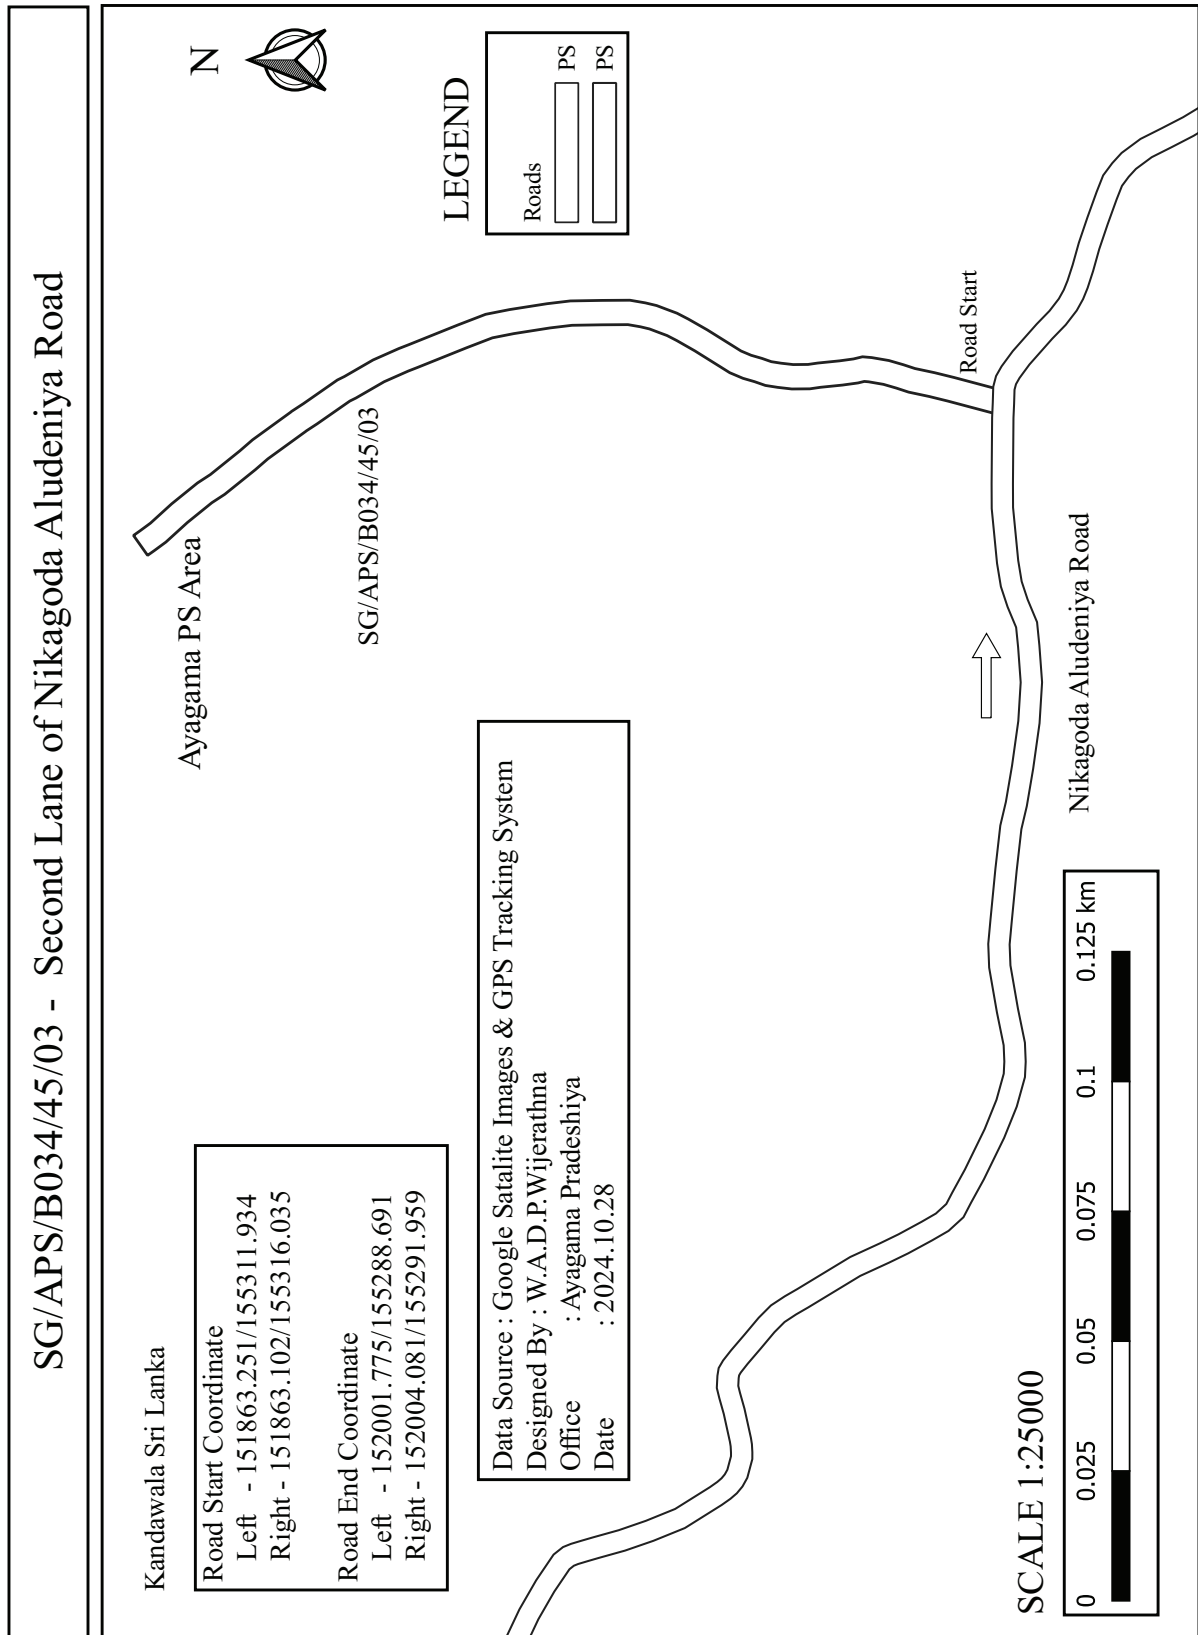


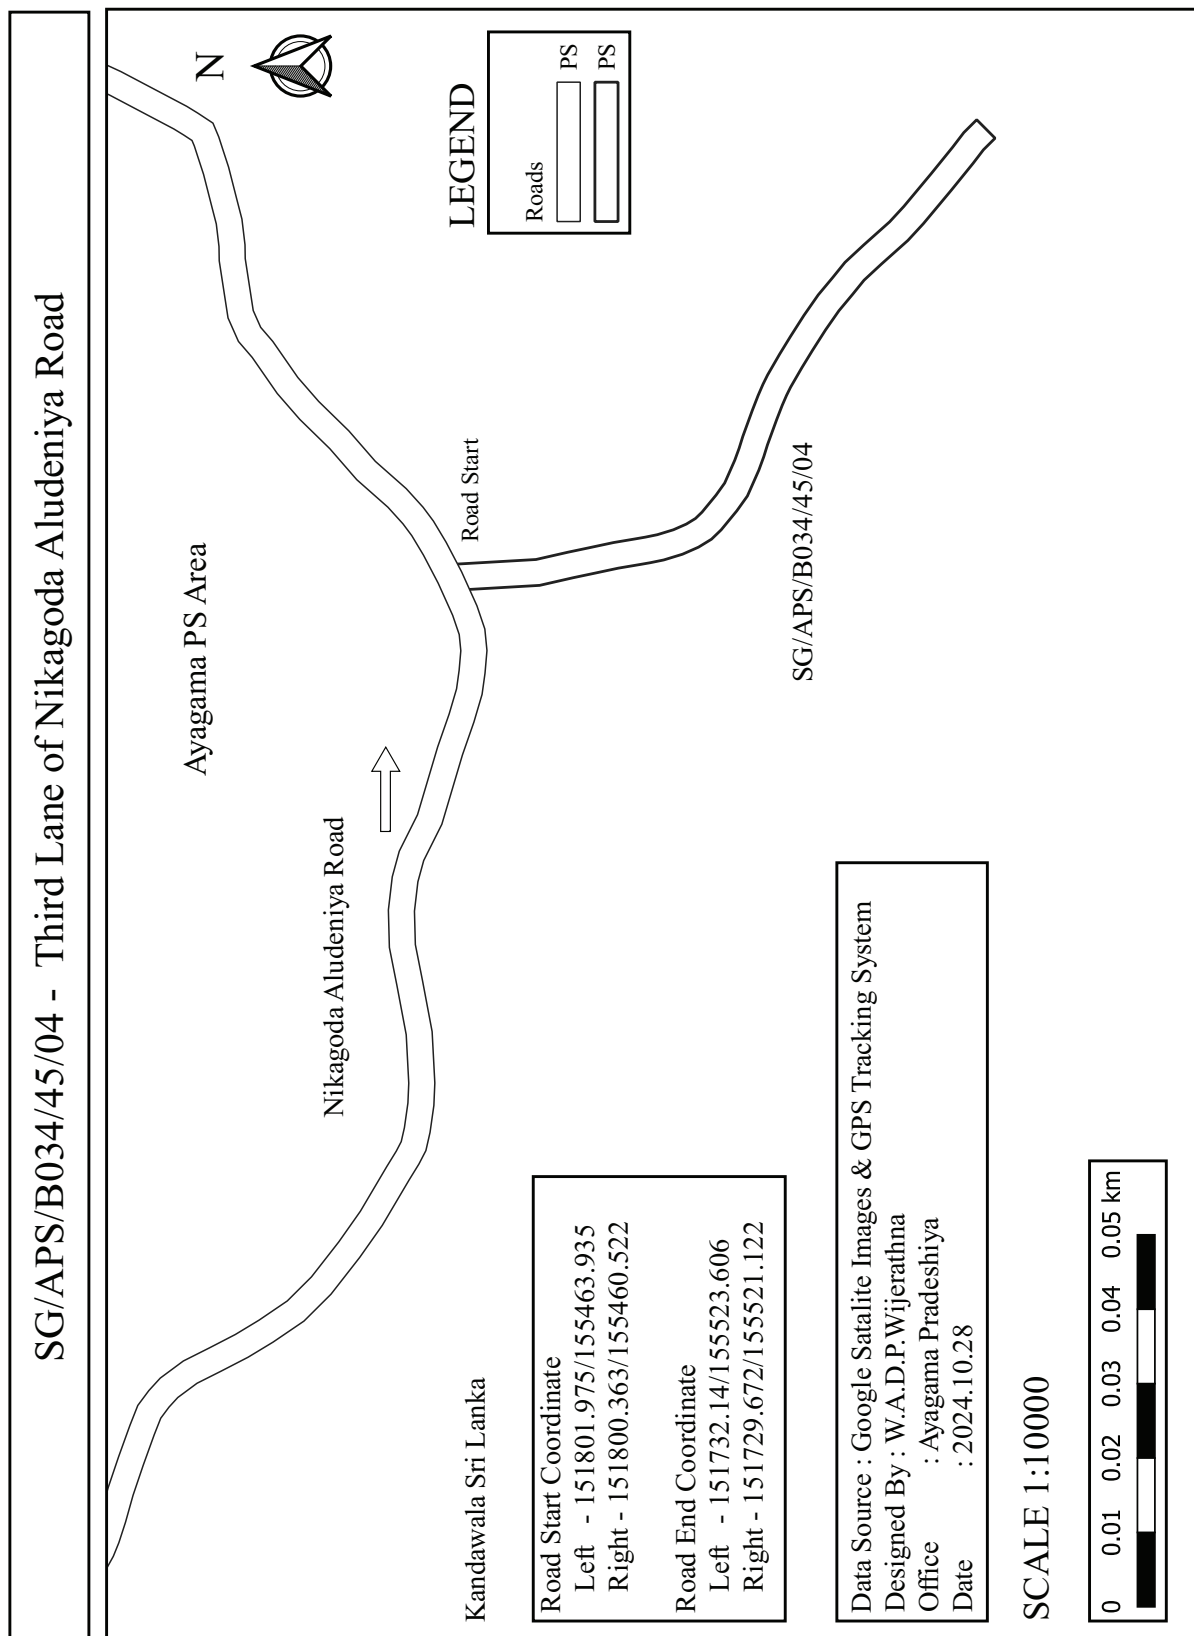


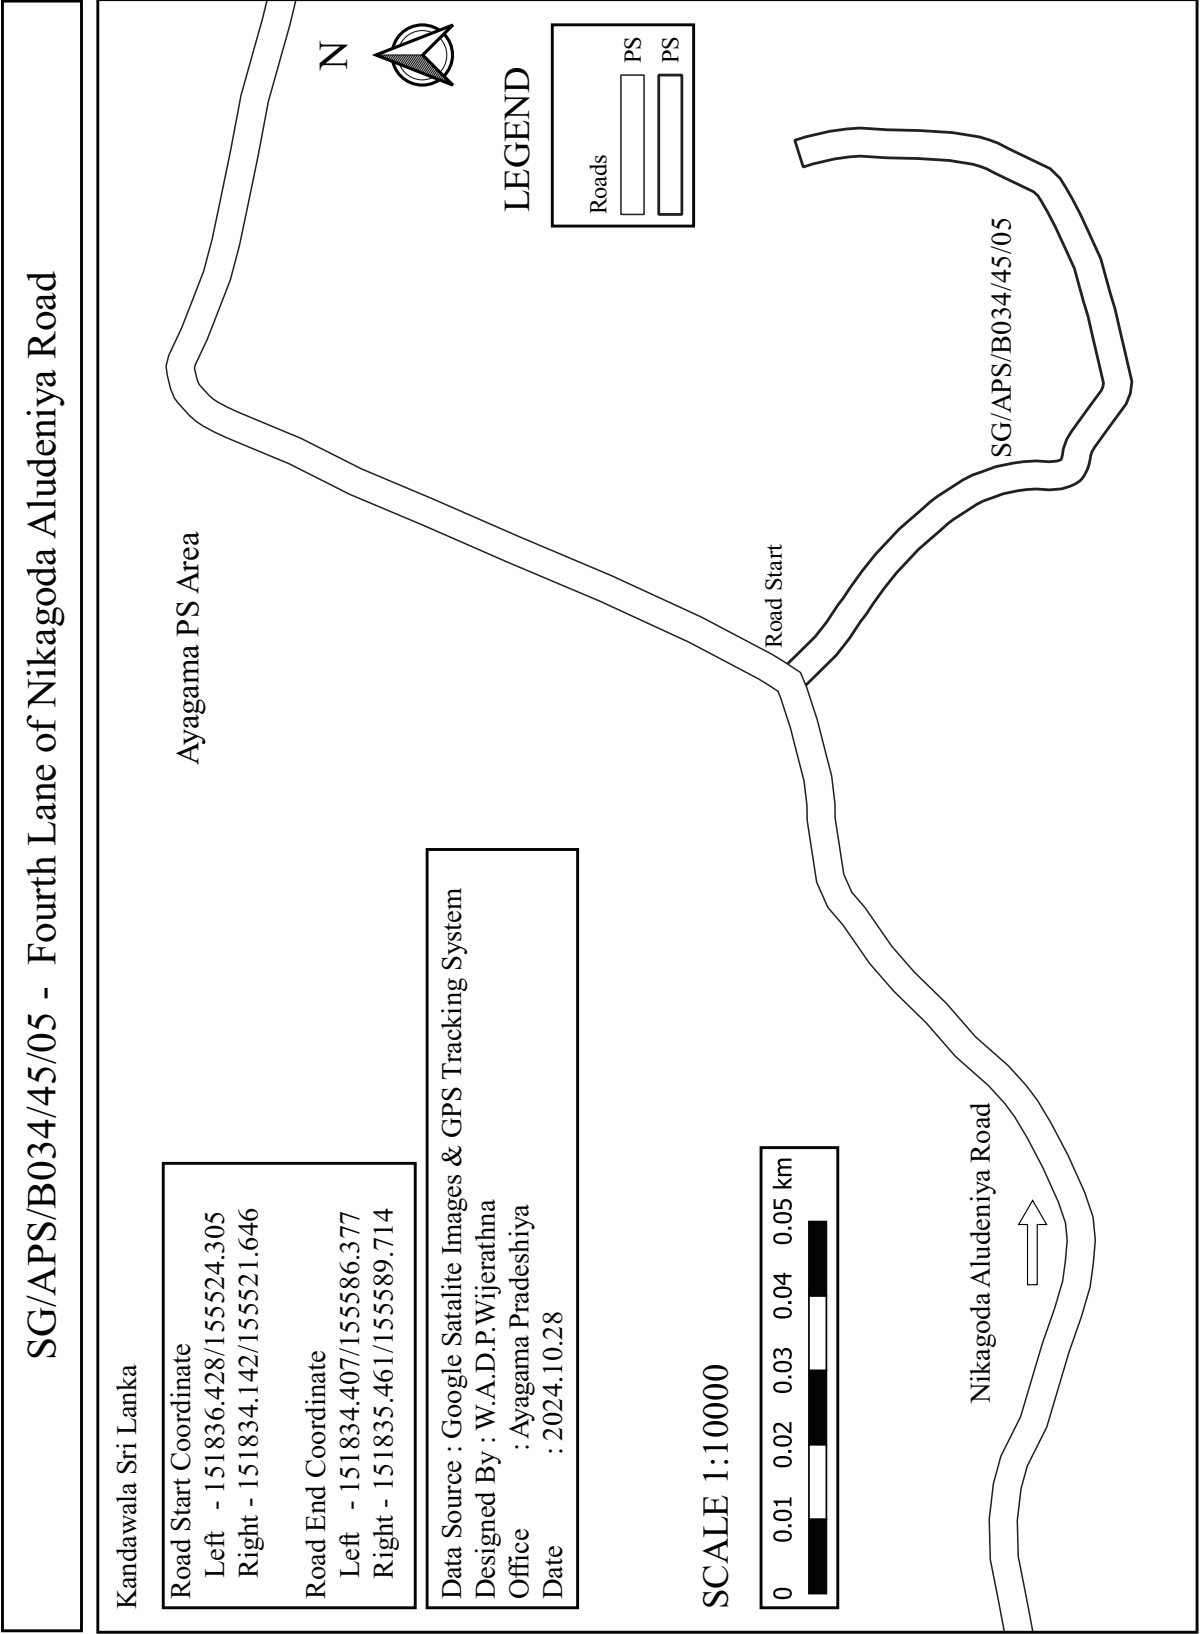


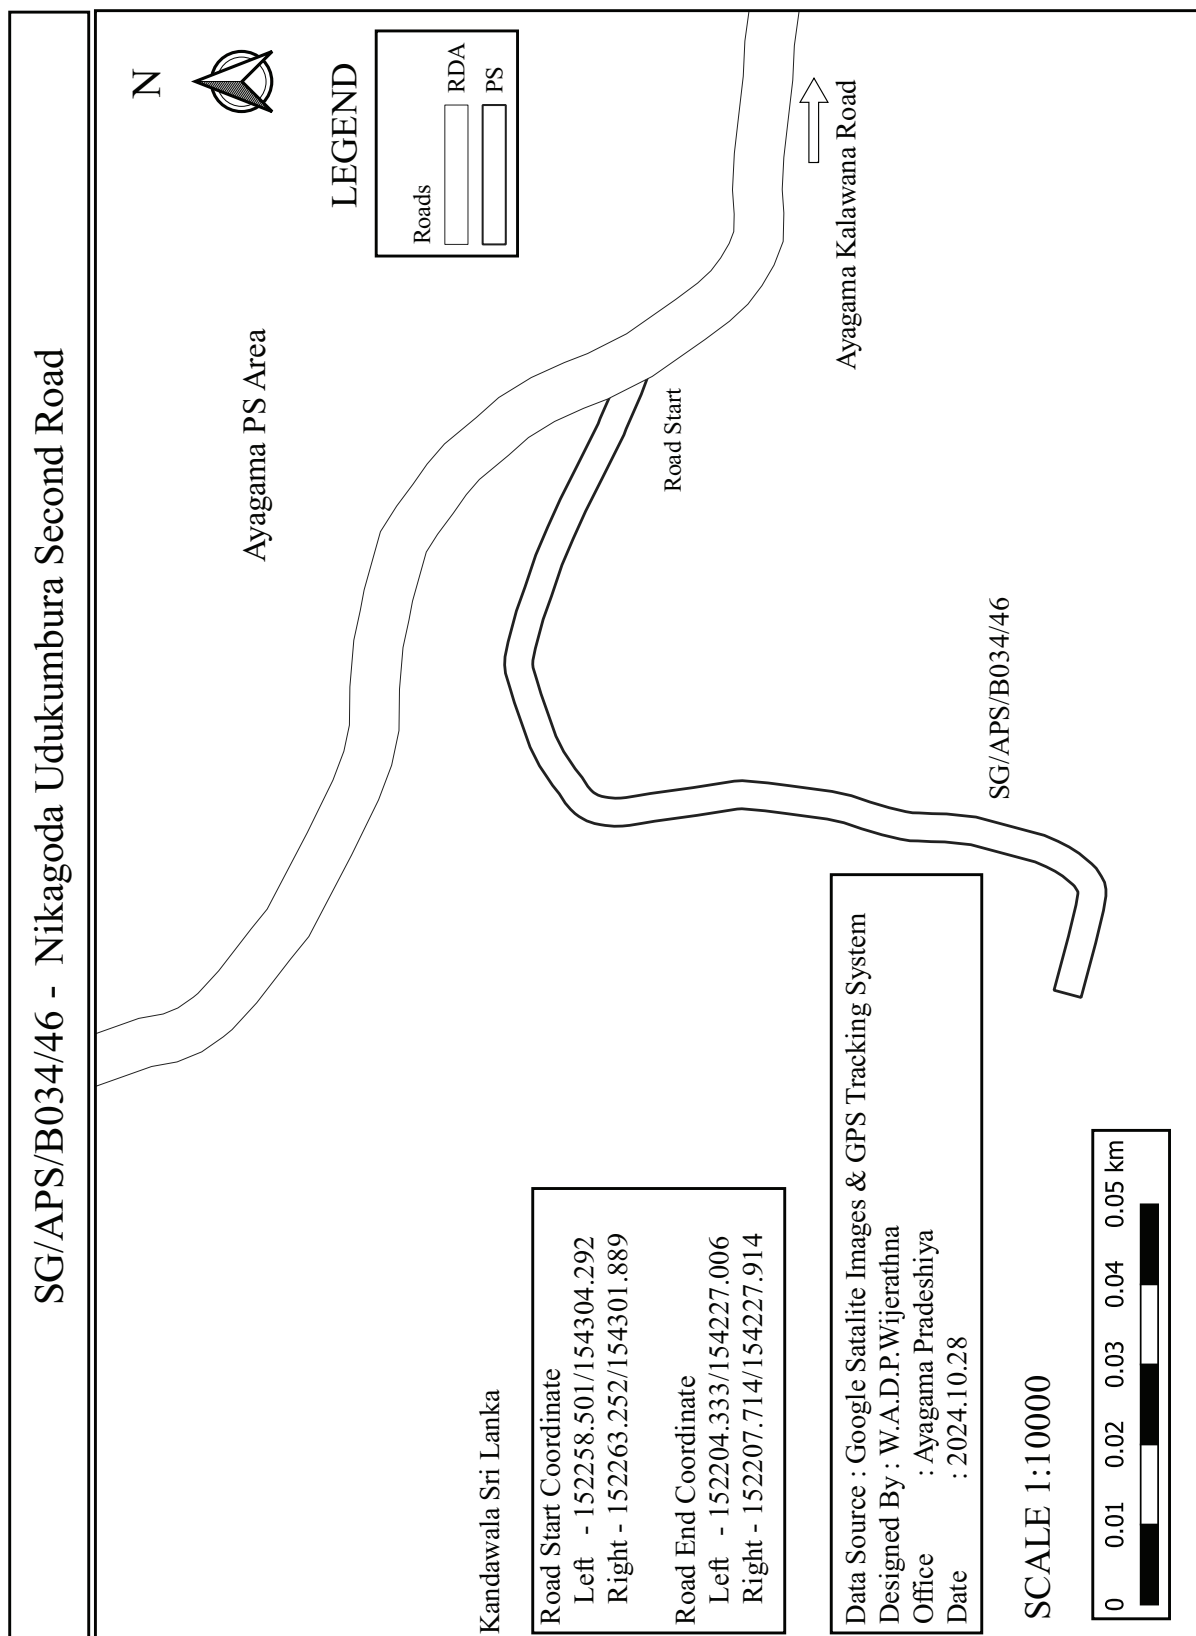


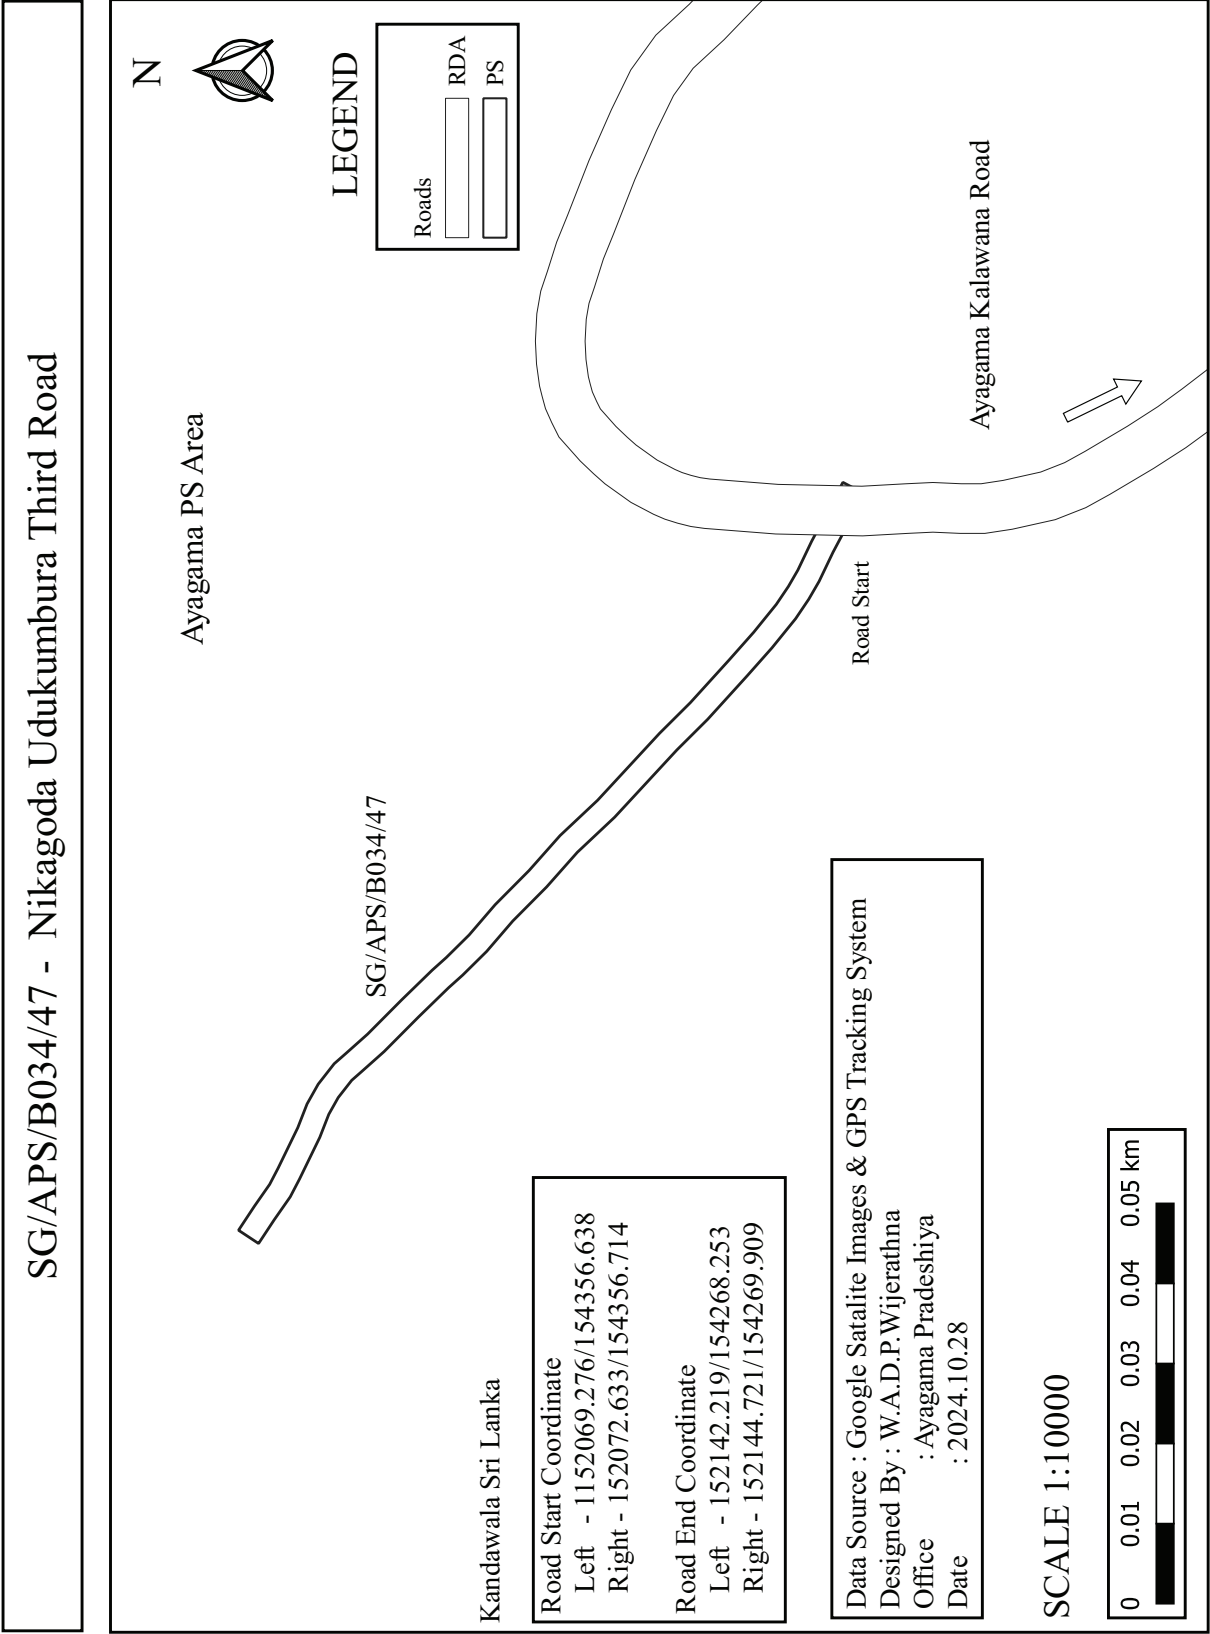


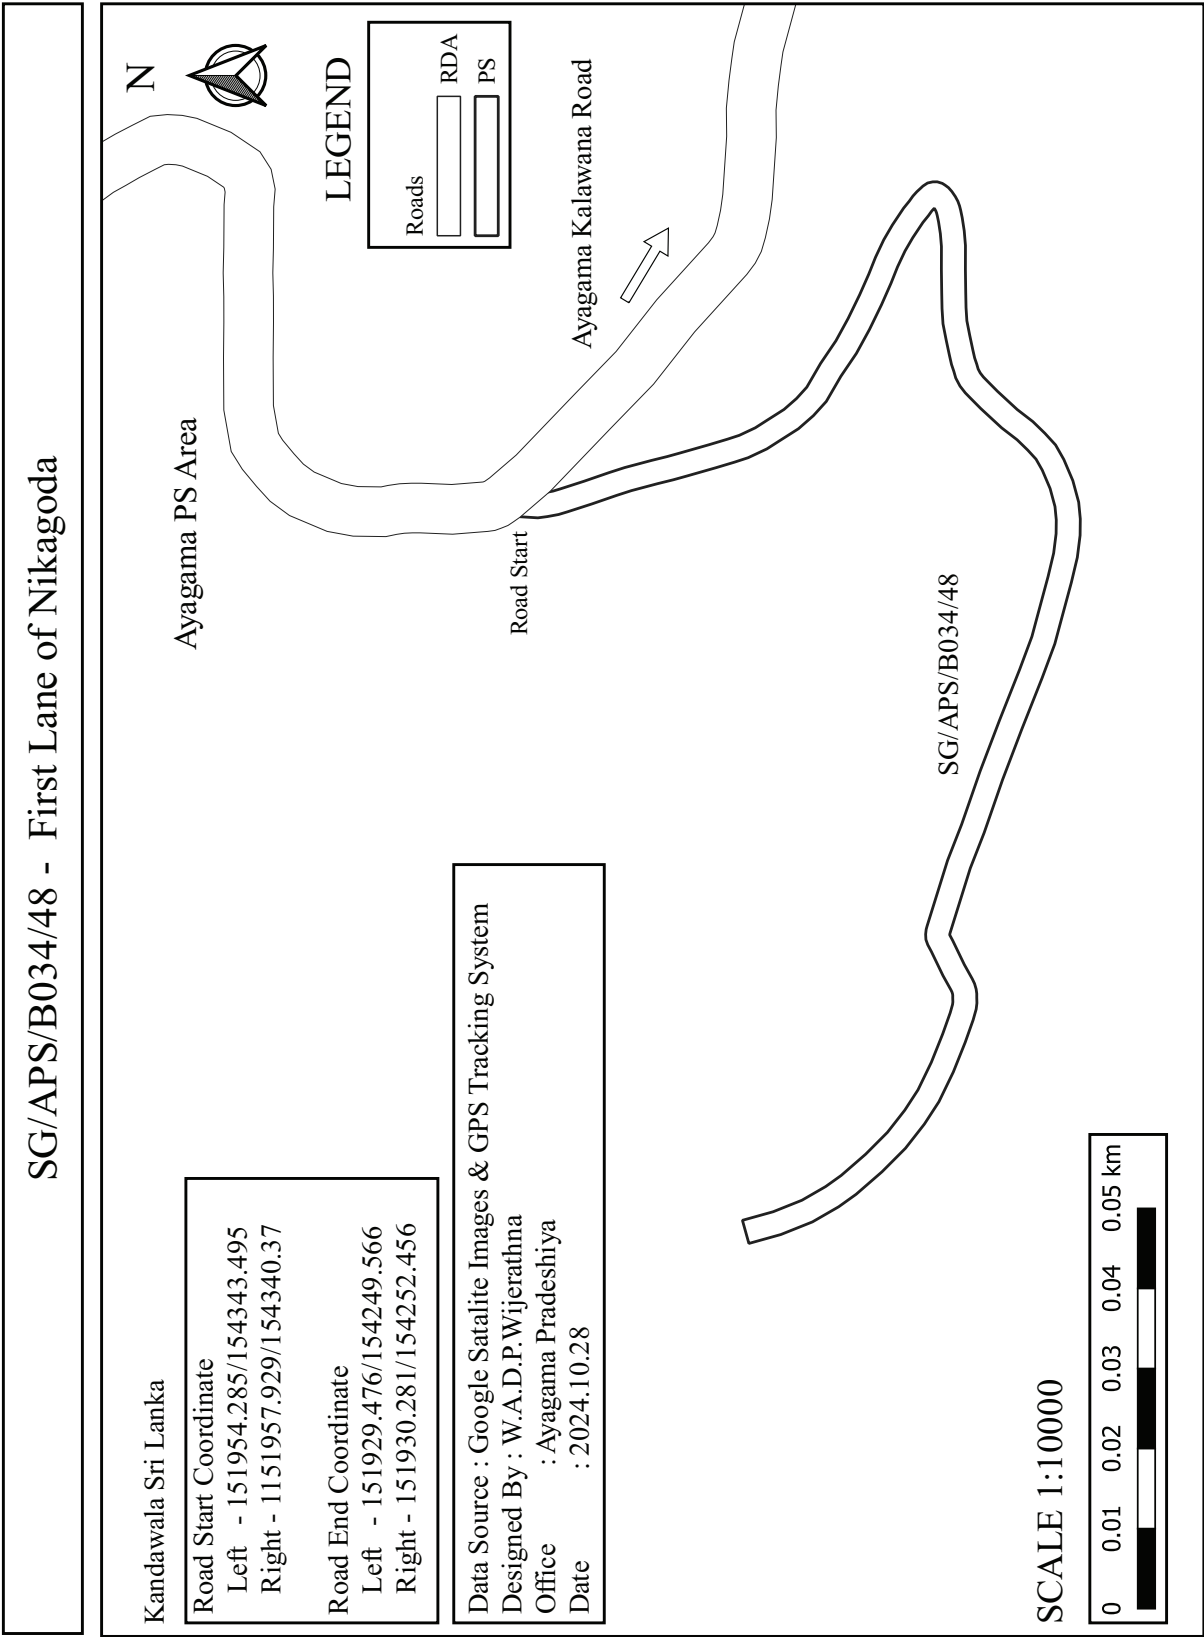


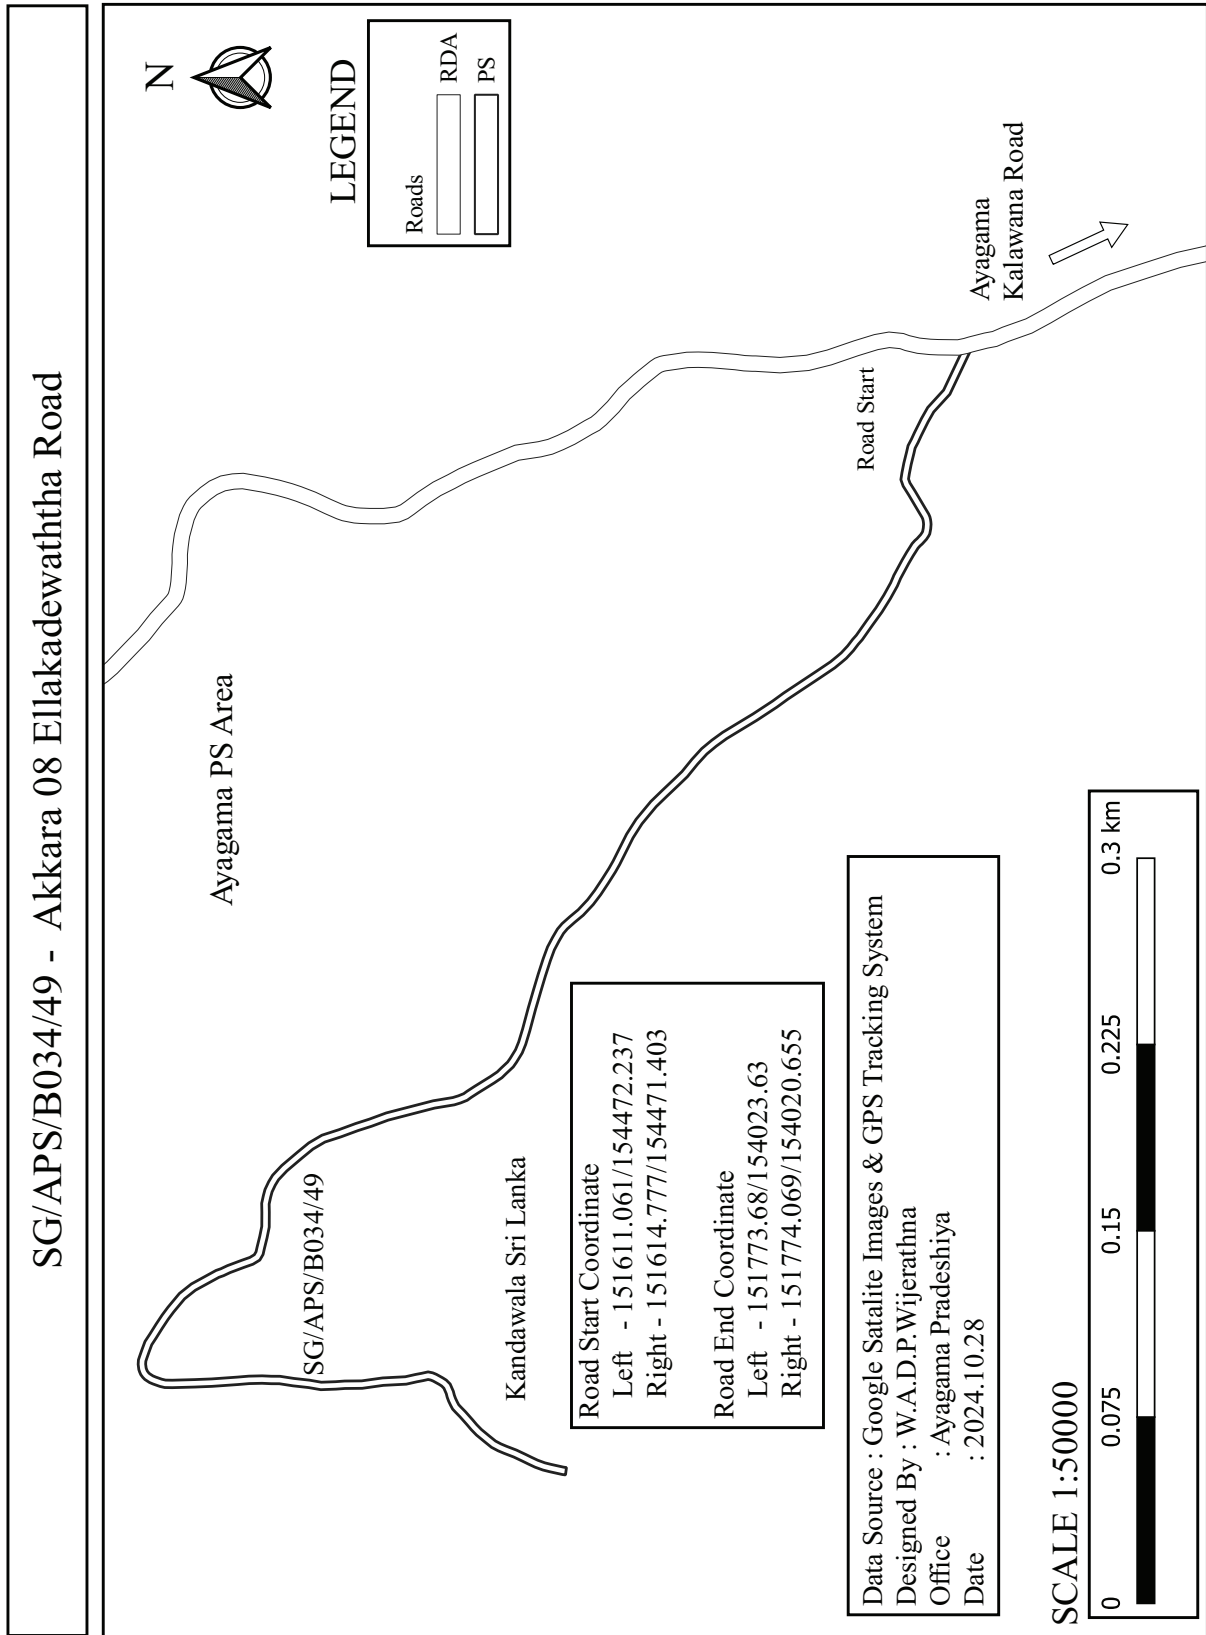


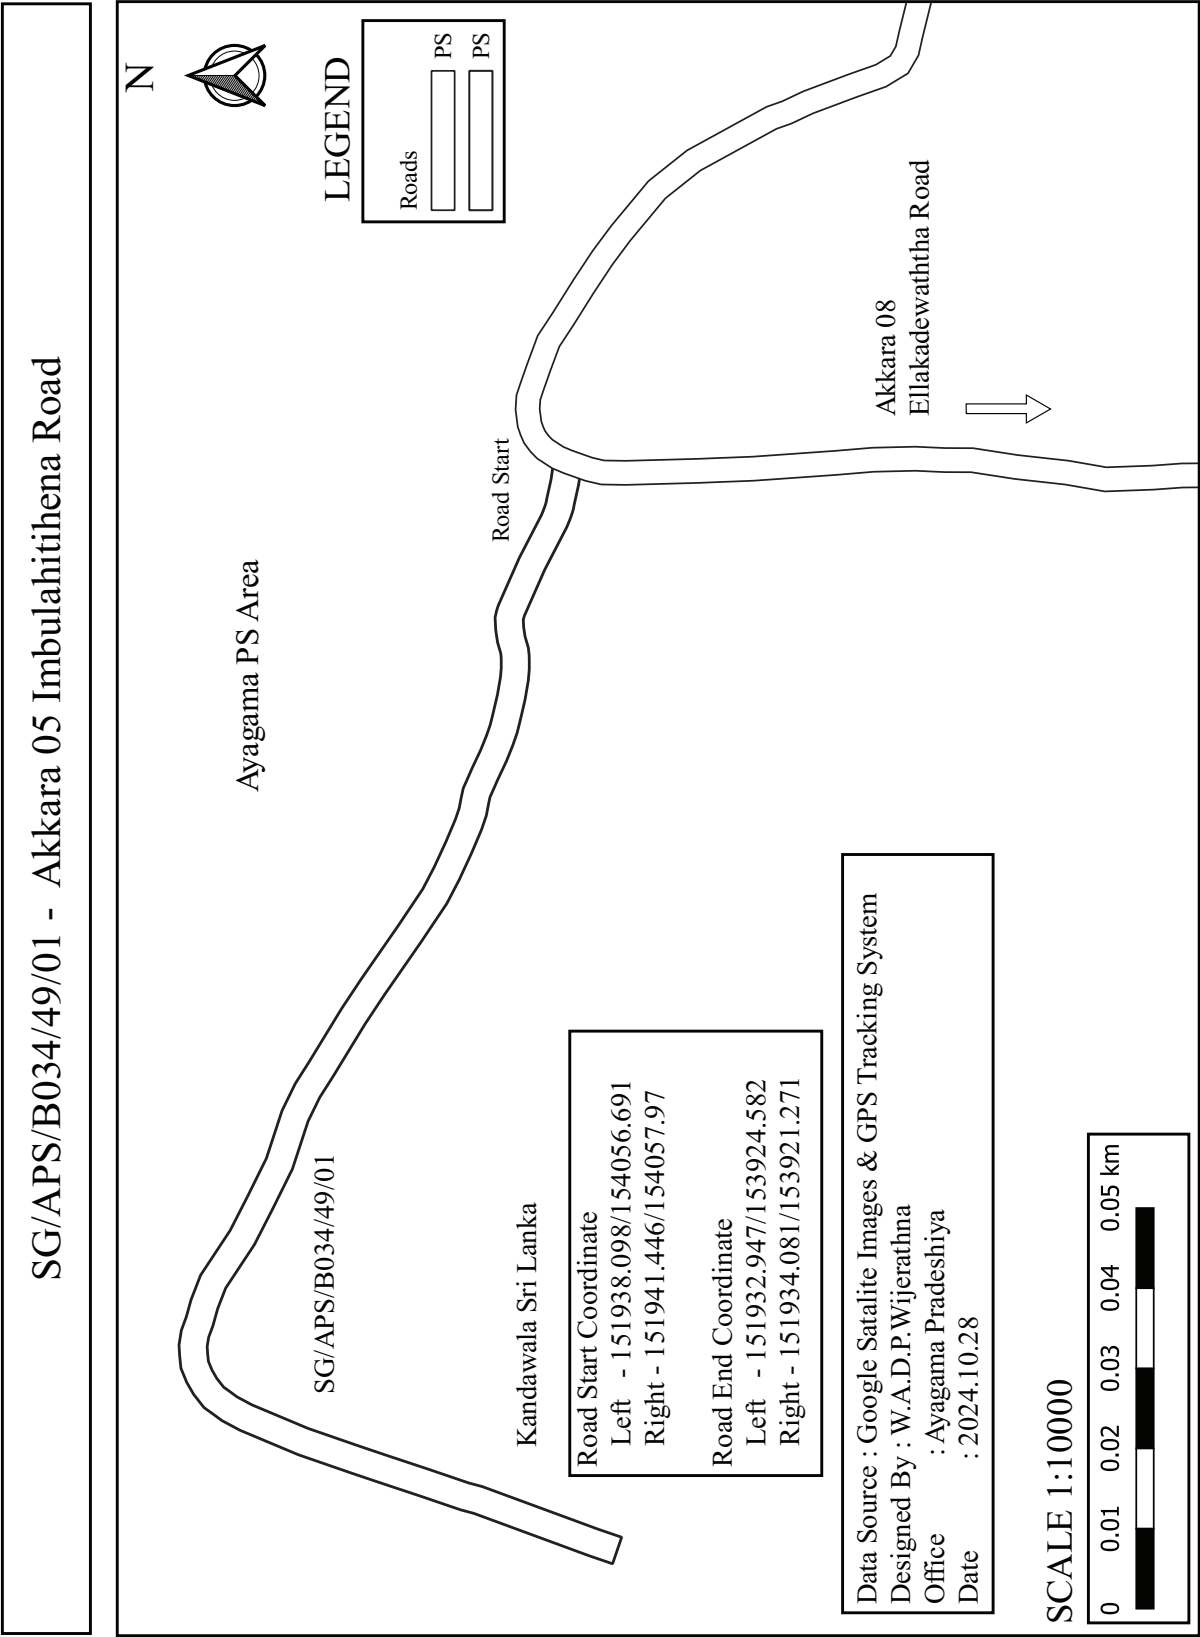


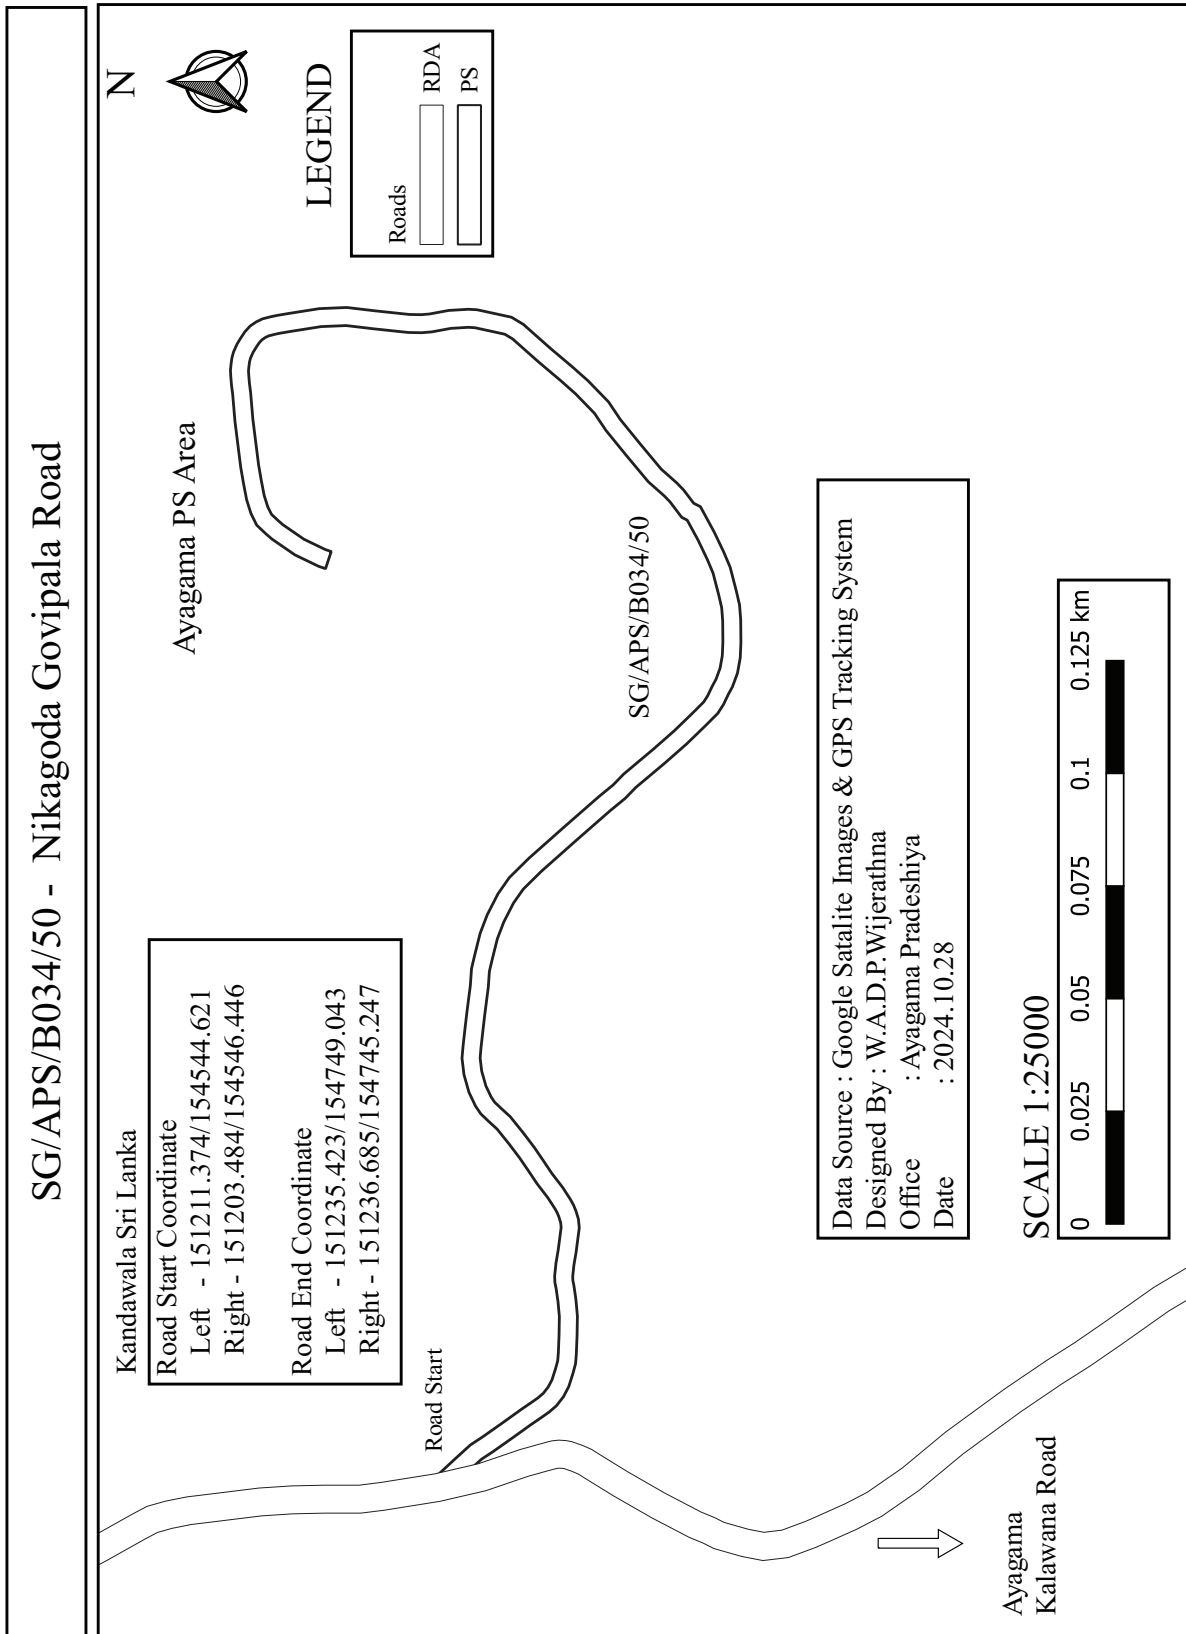

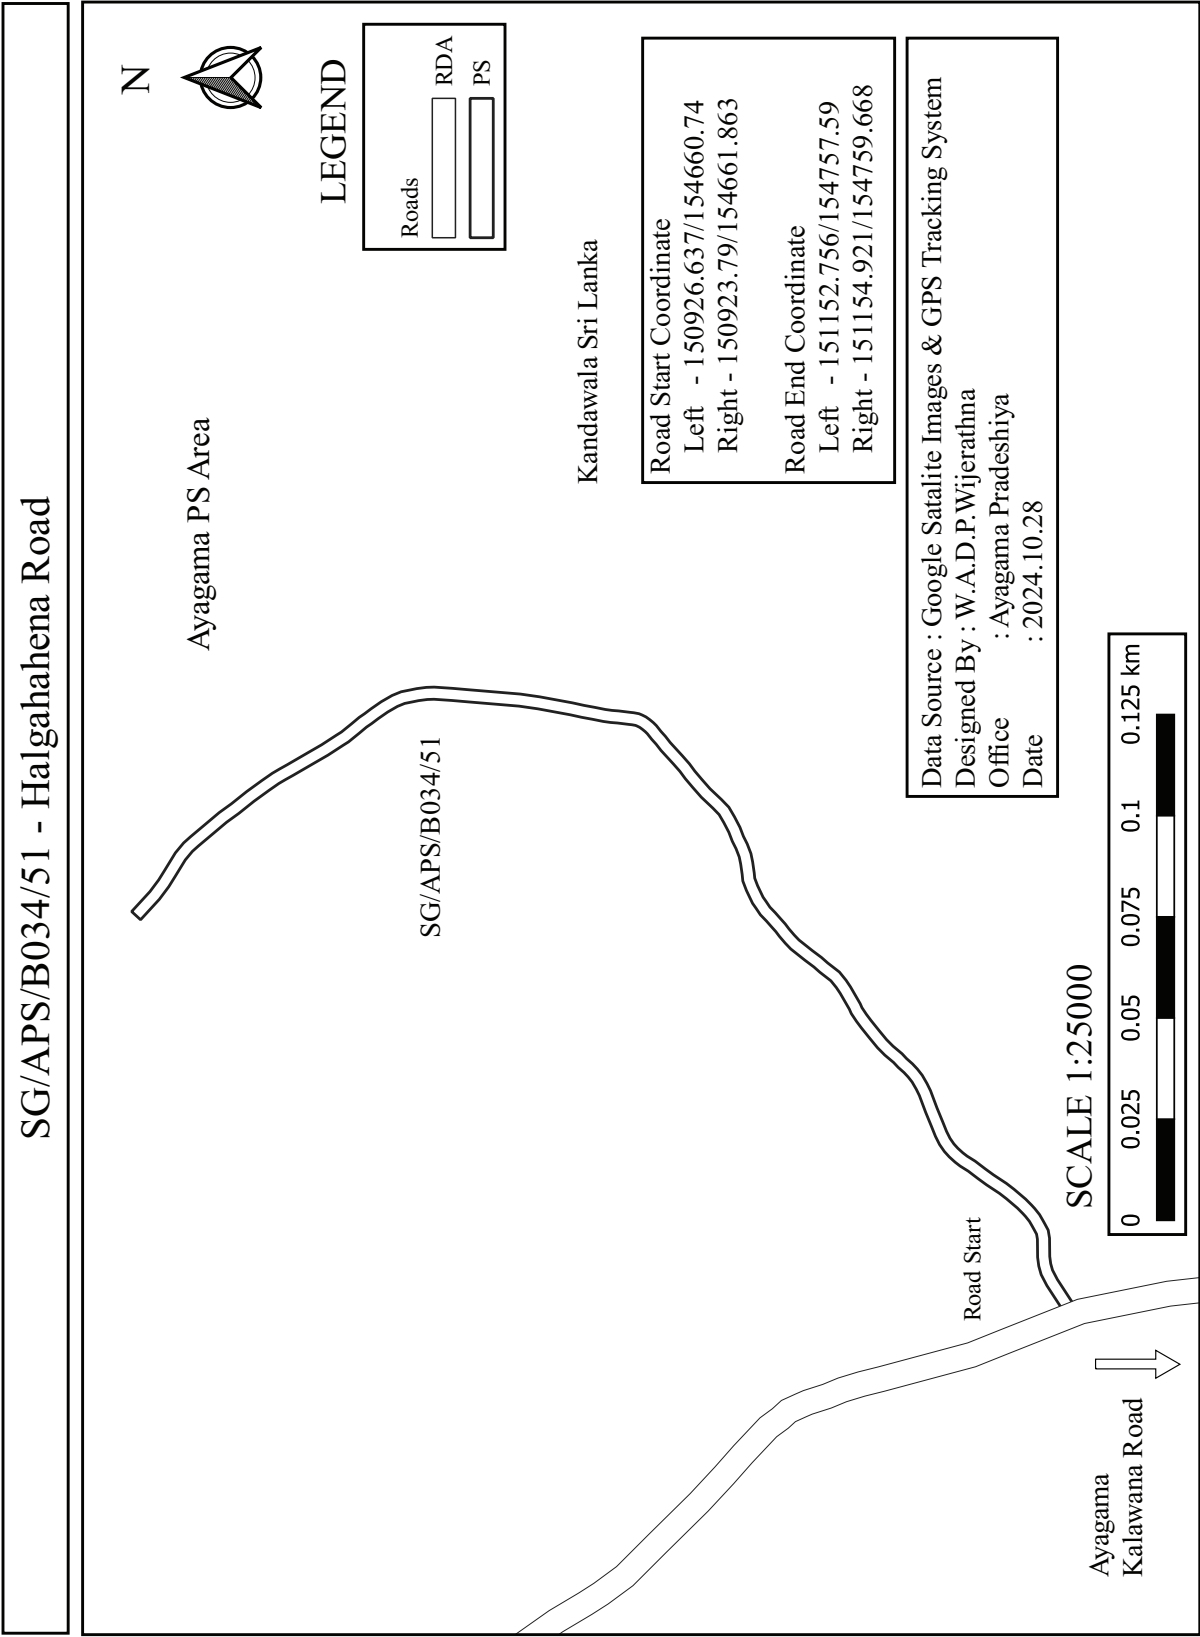

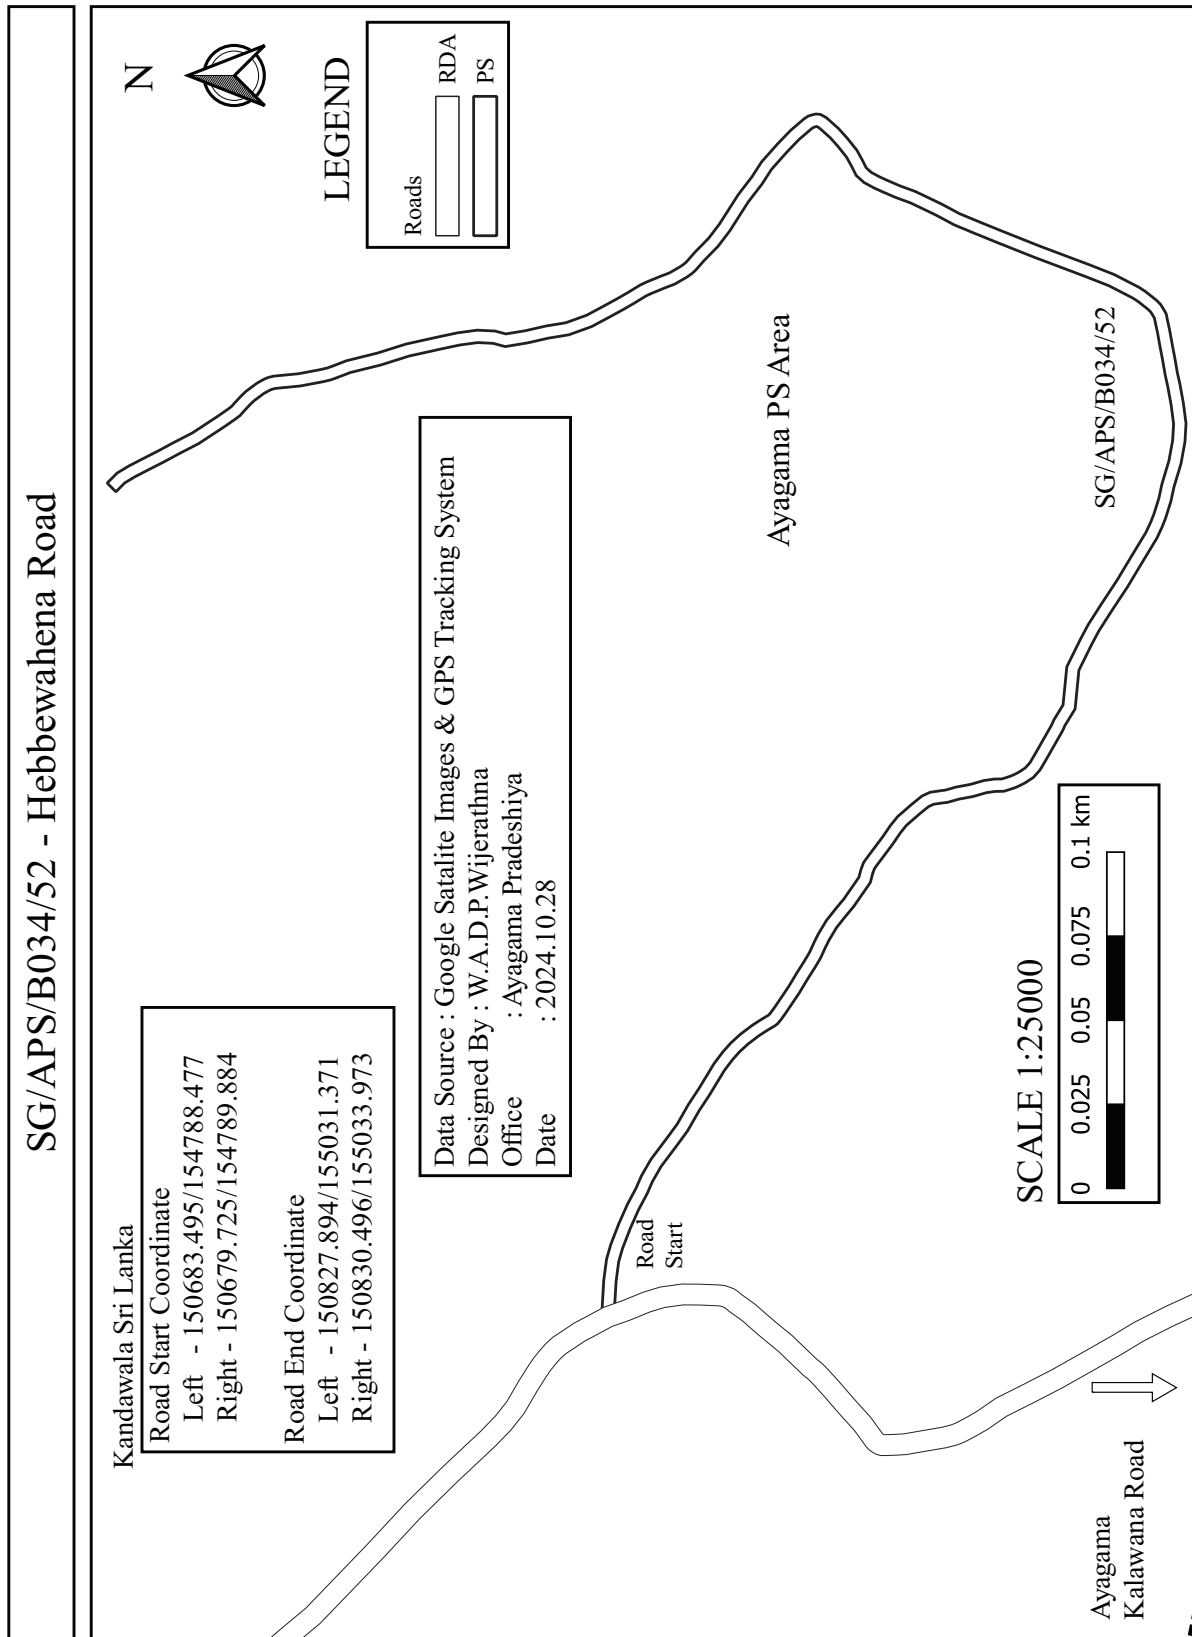


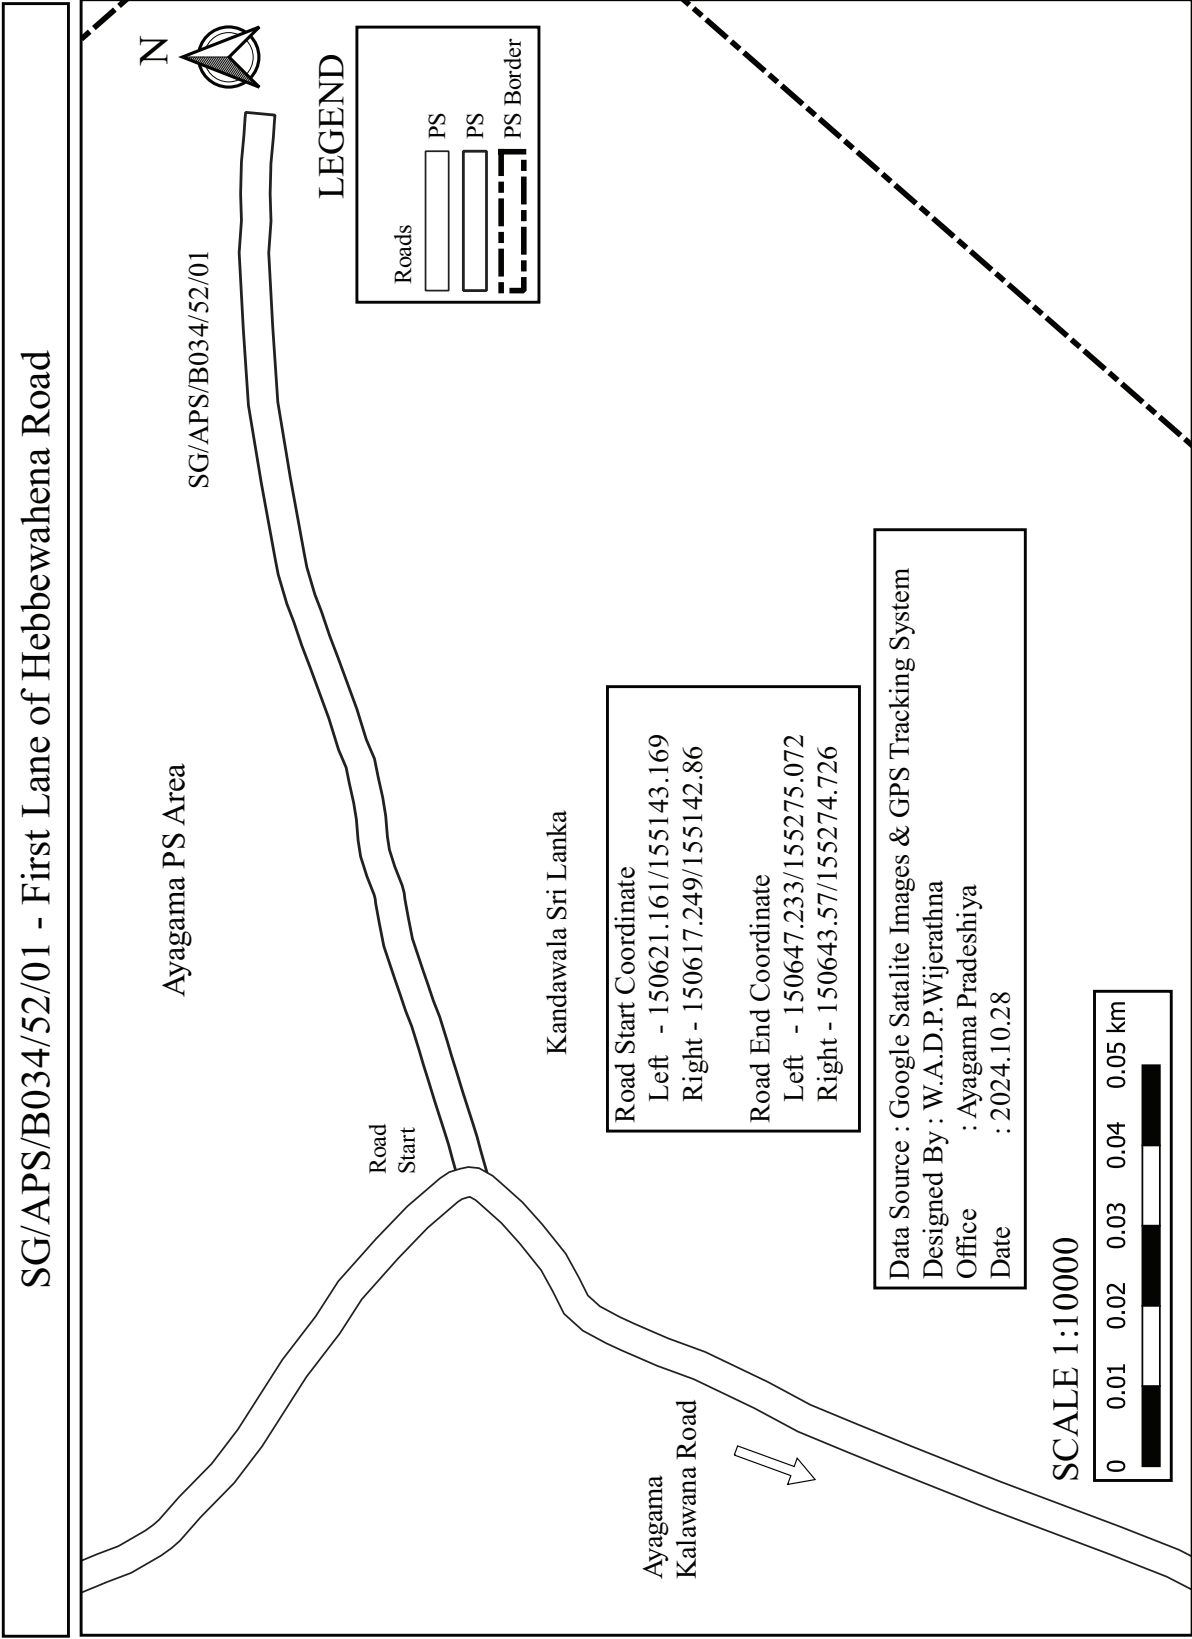


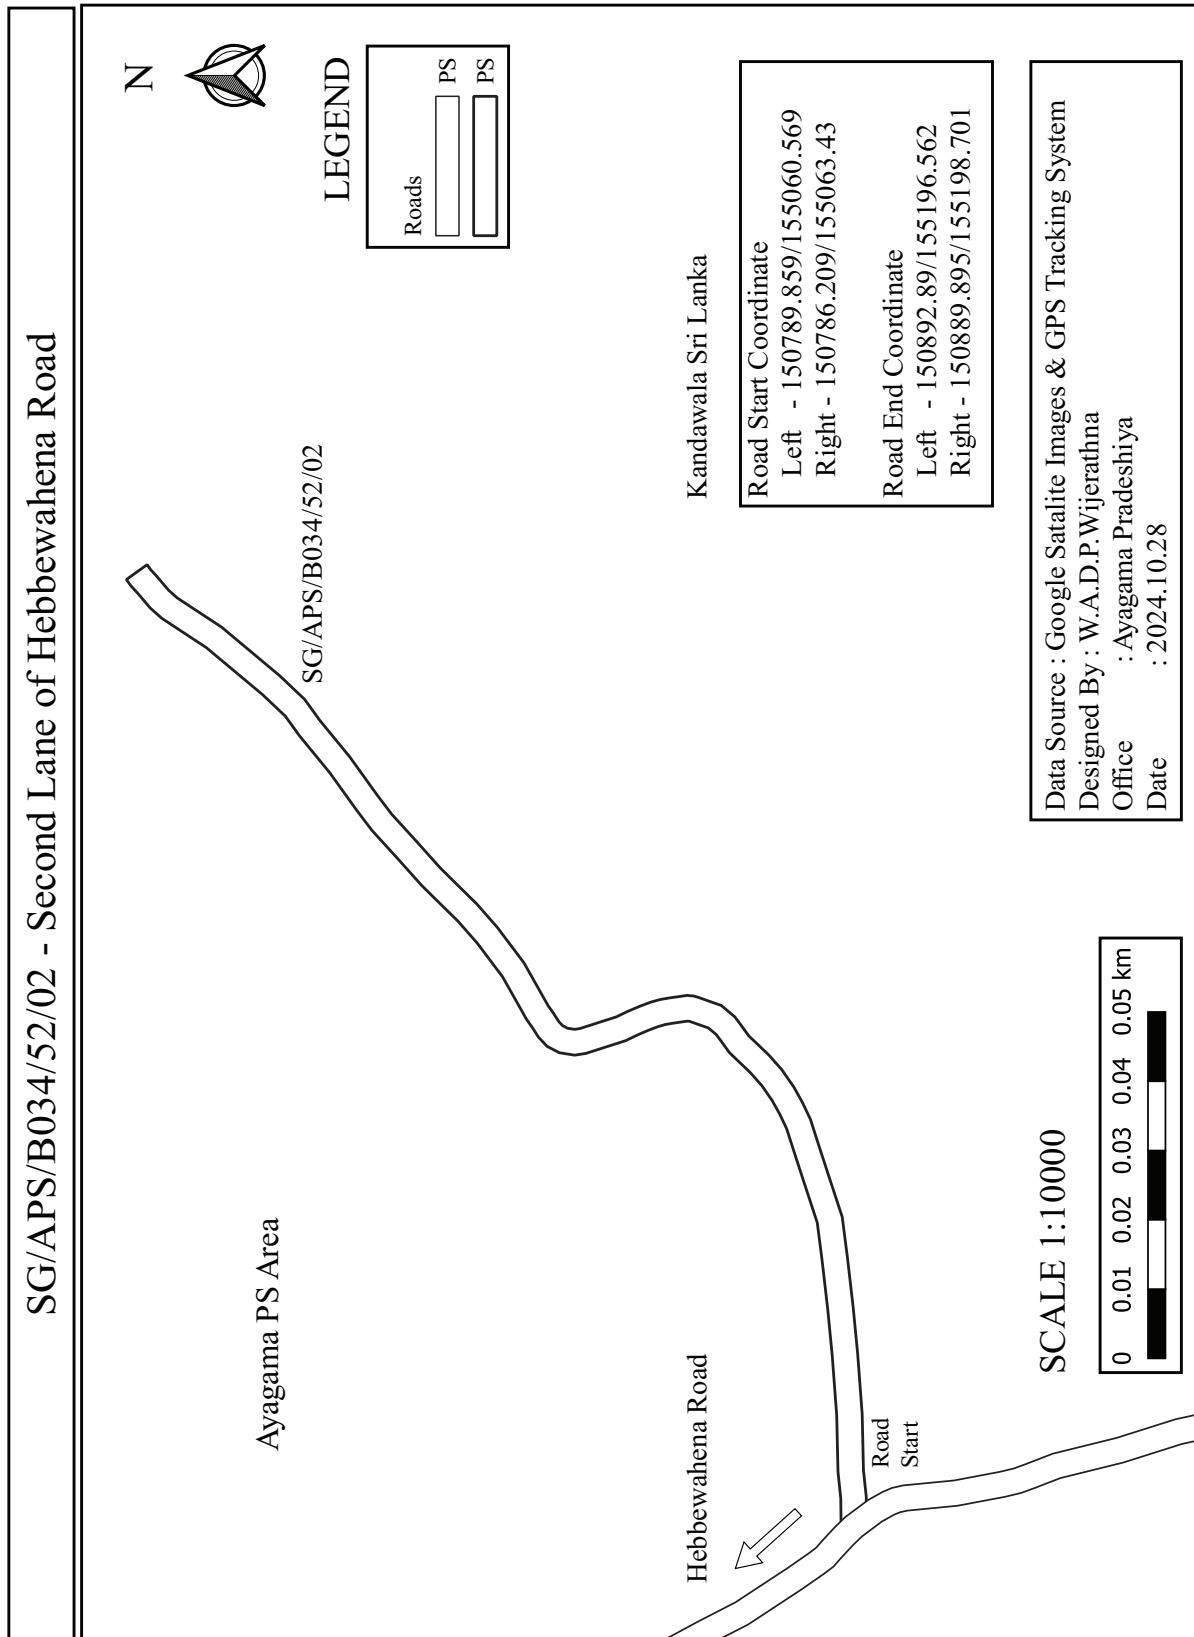



N




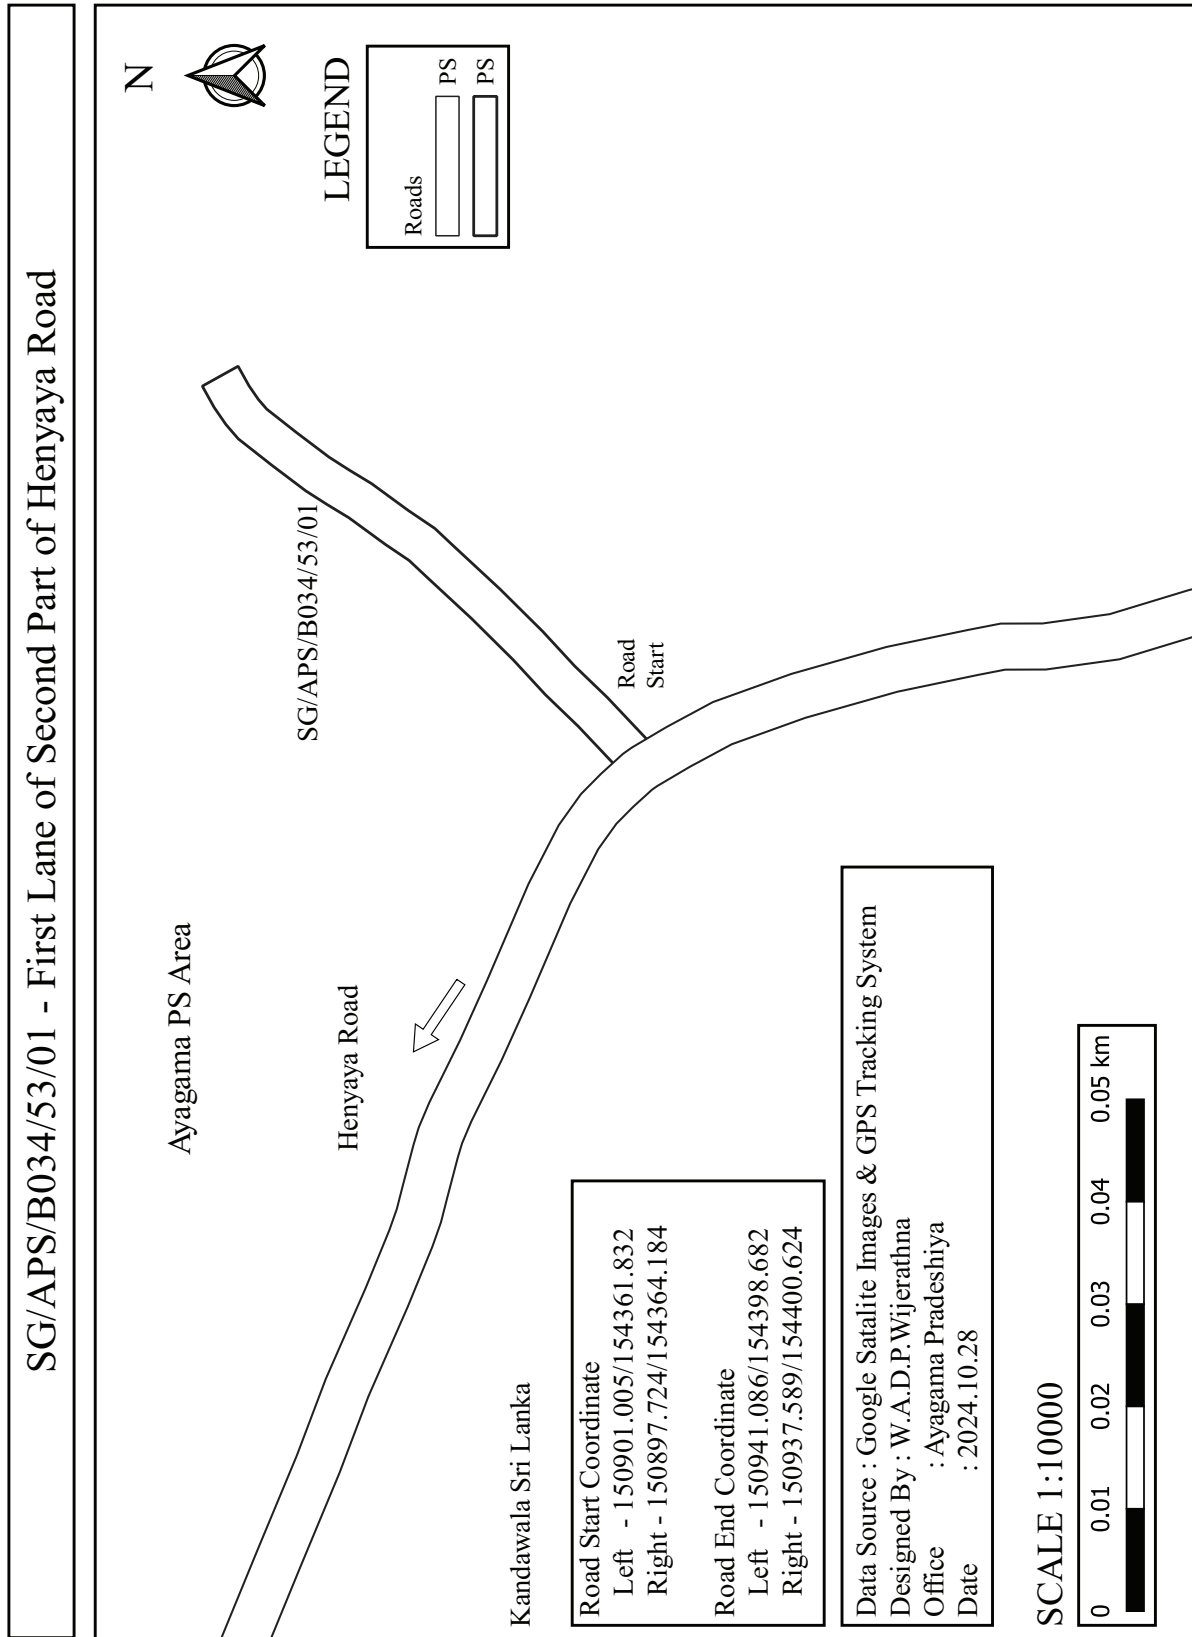


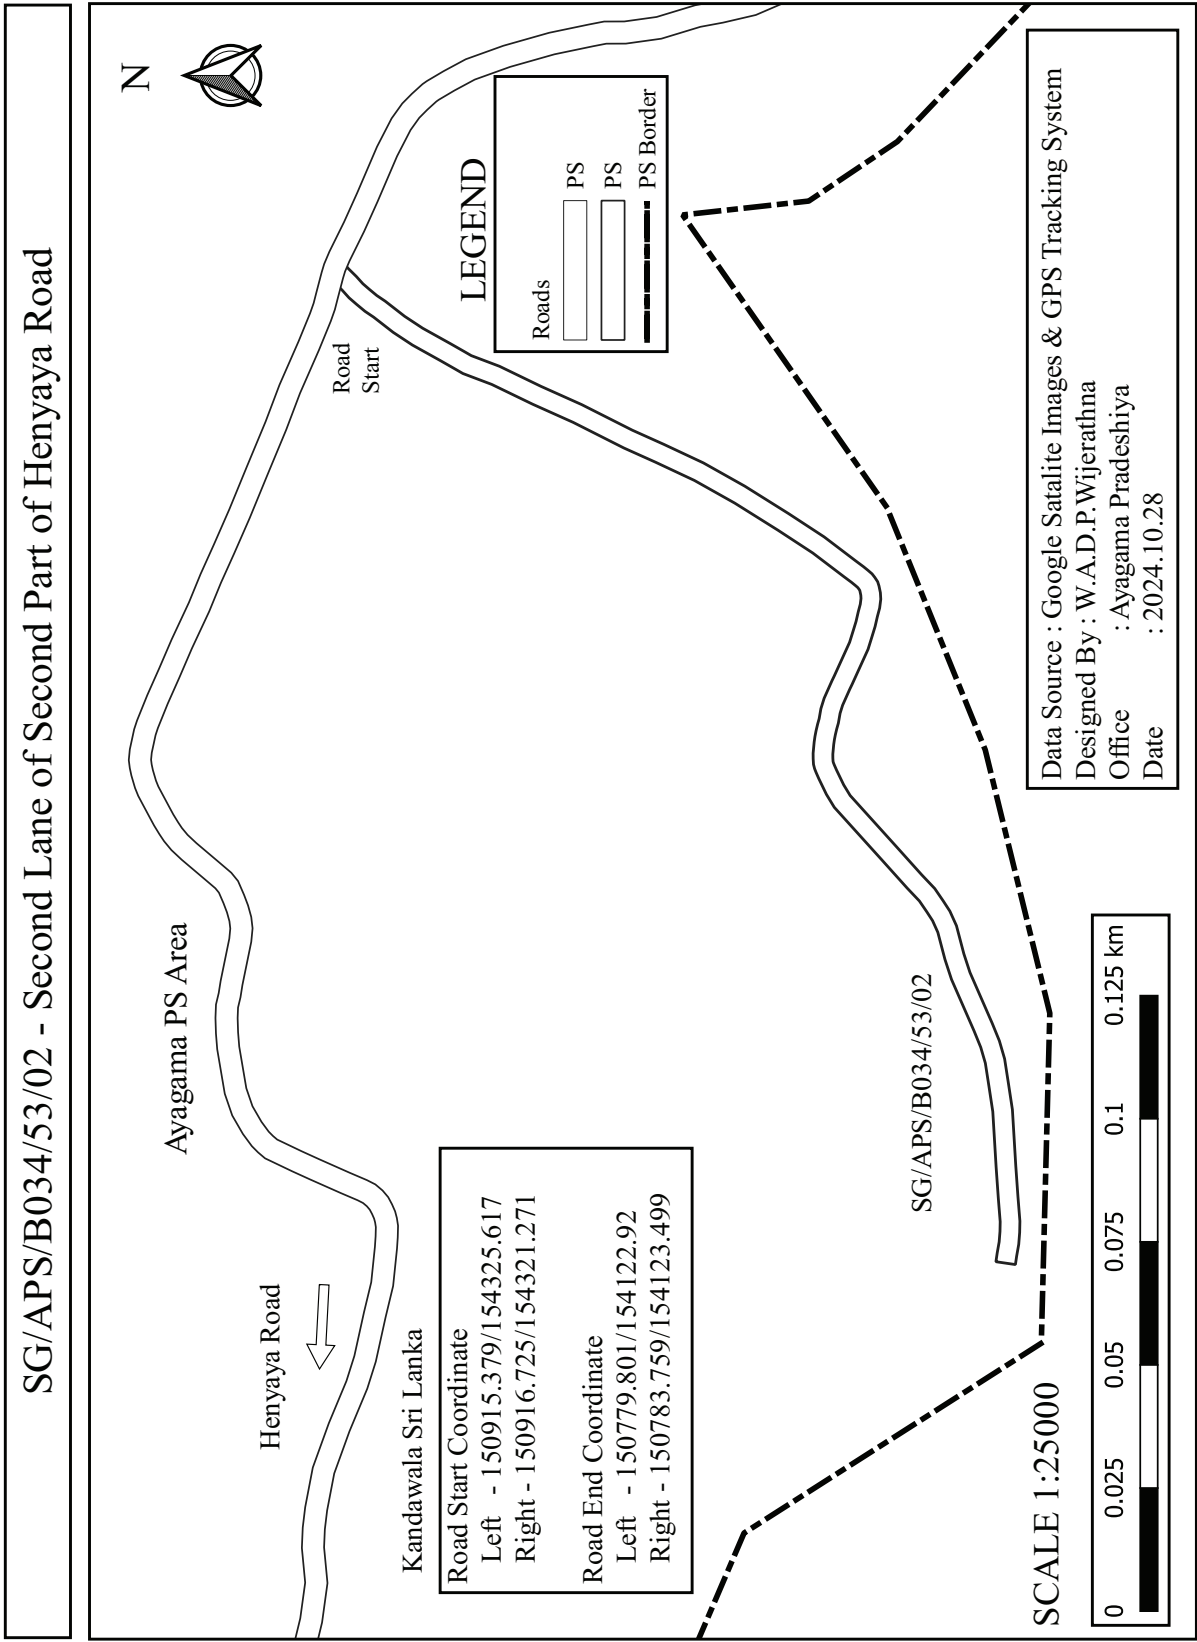


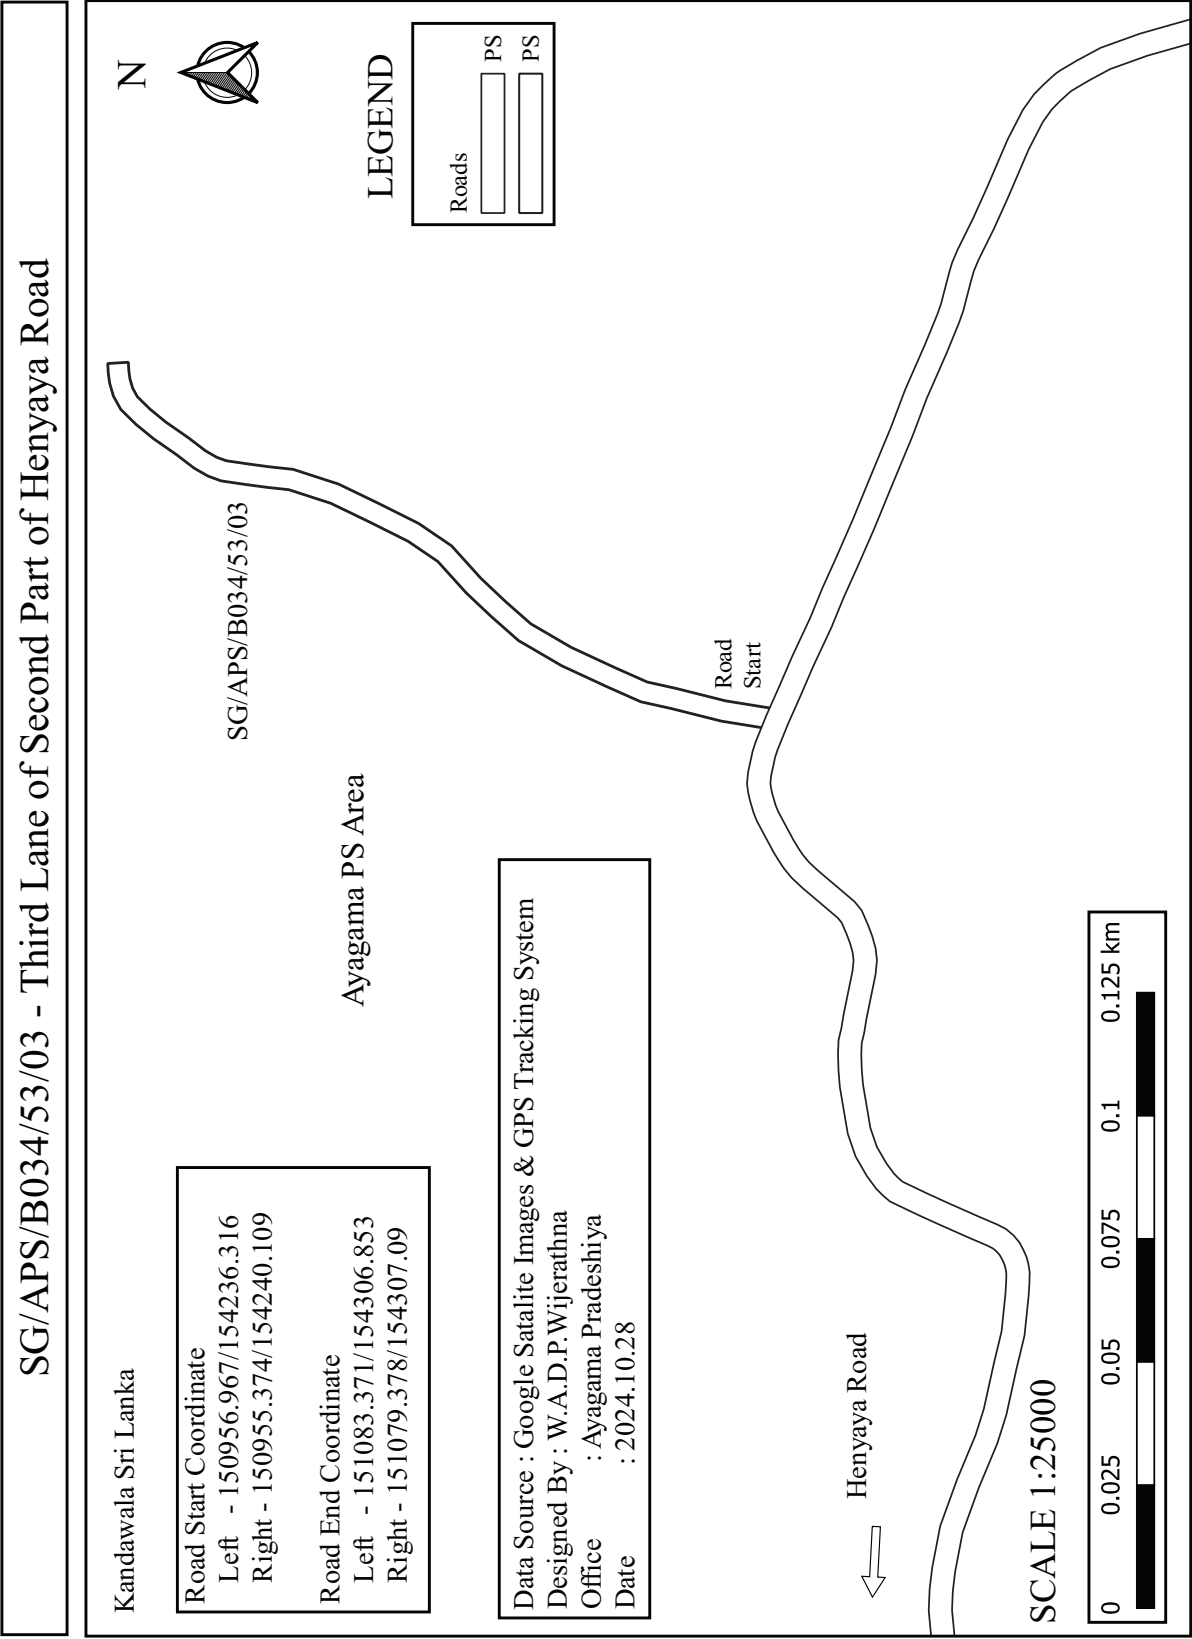


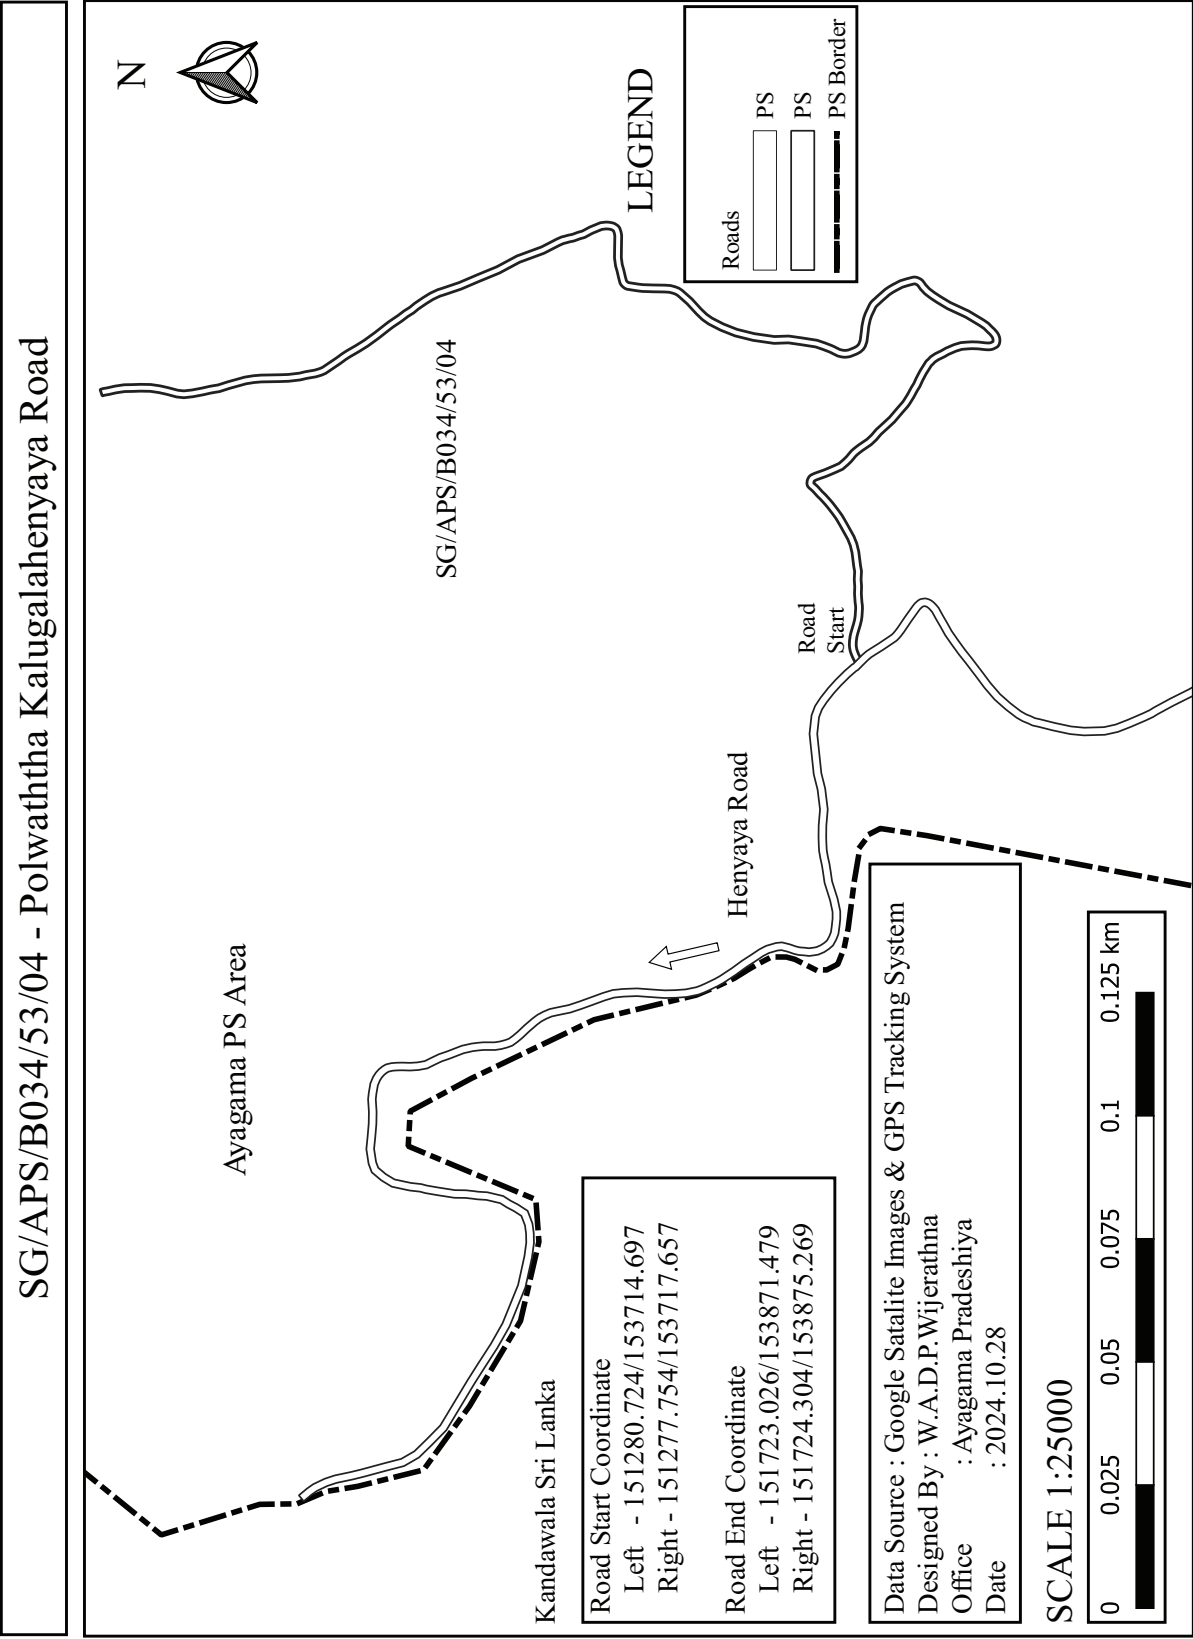


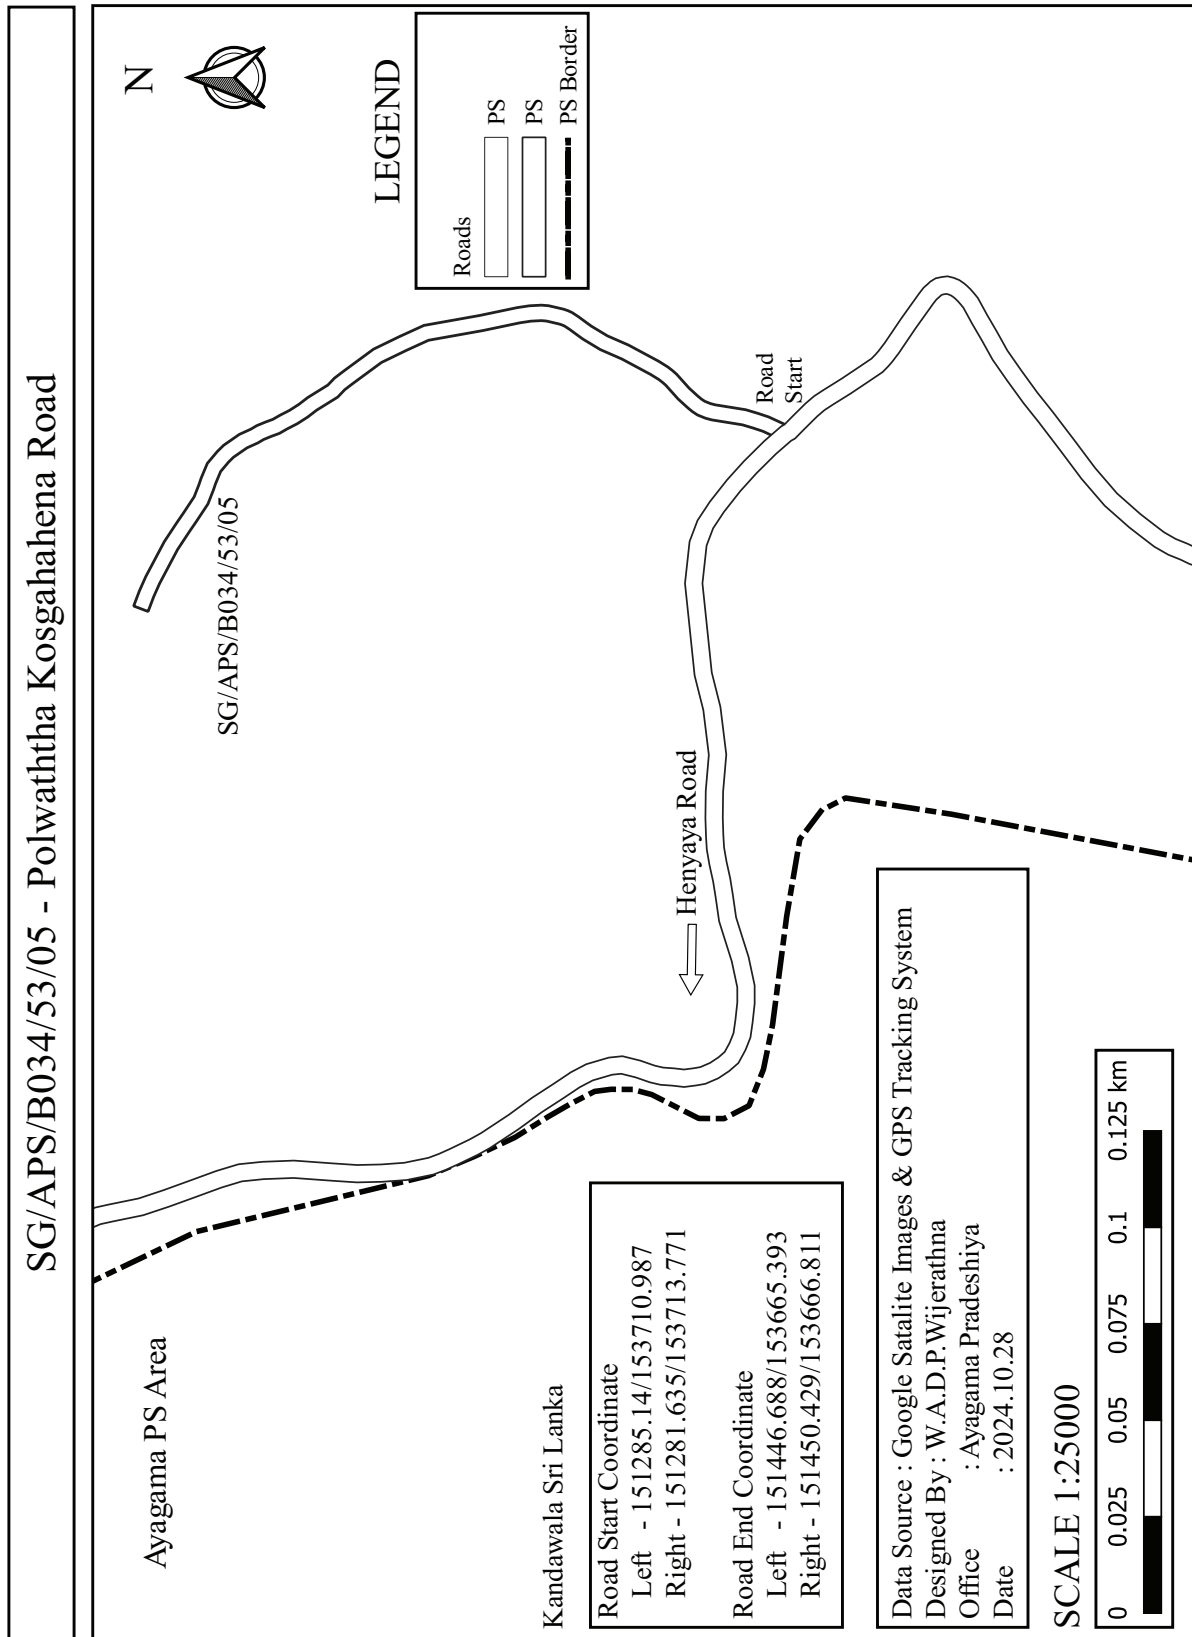


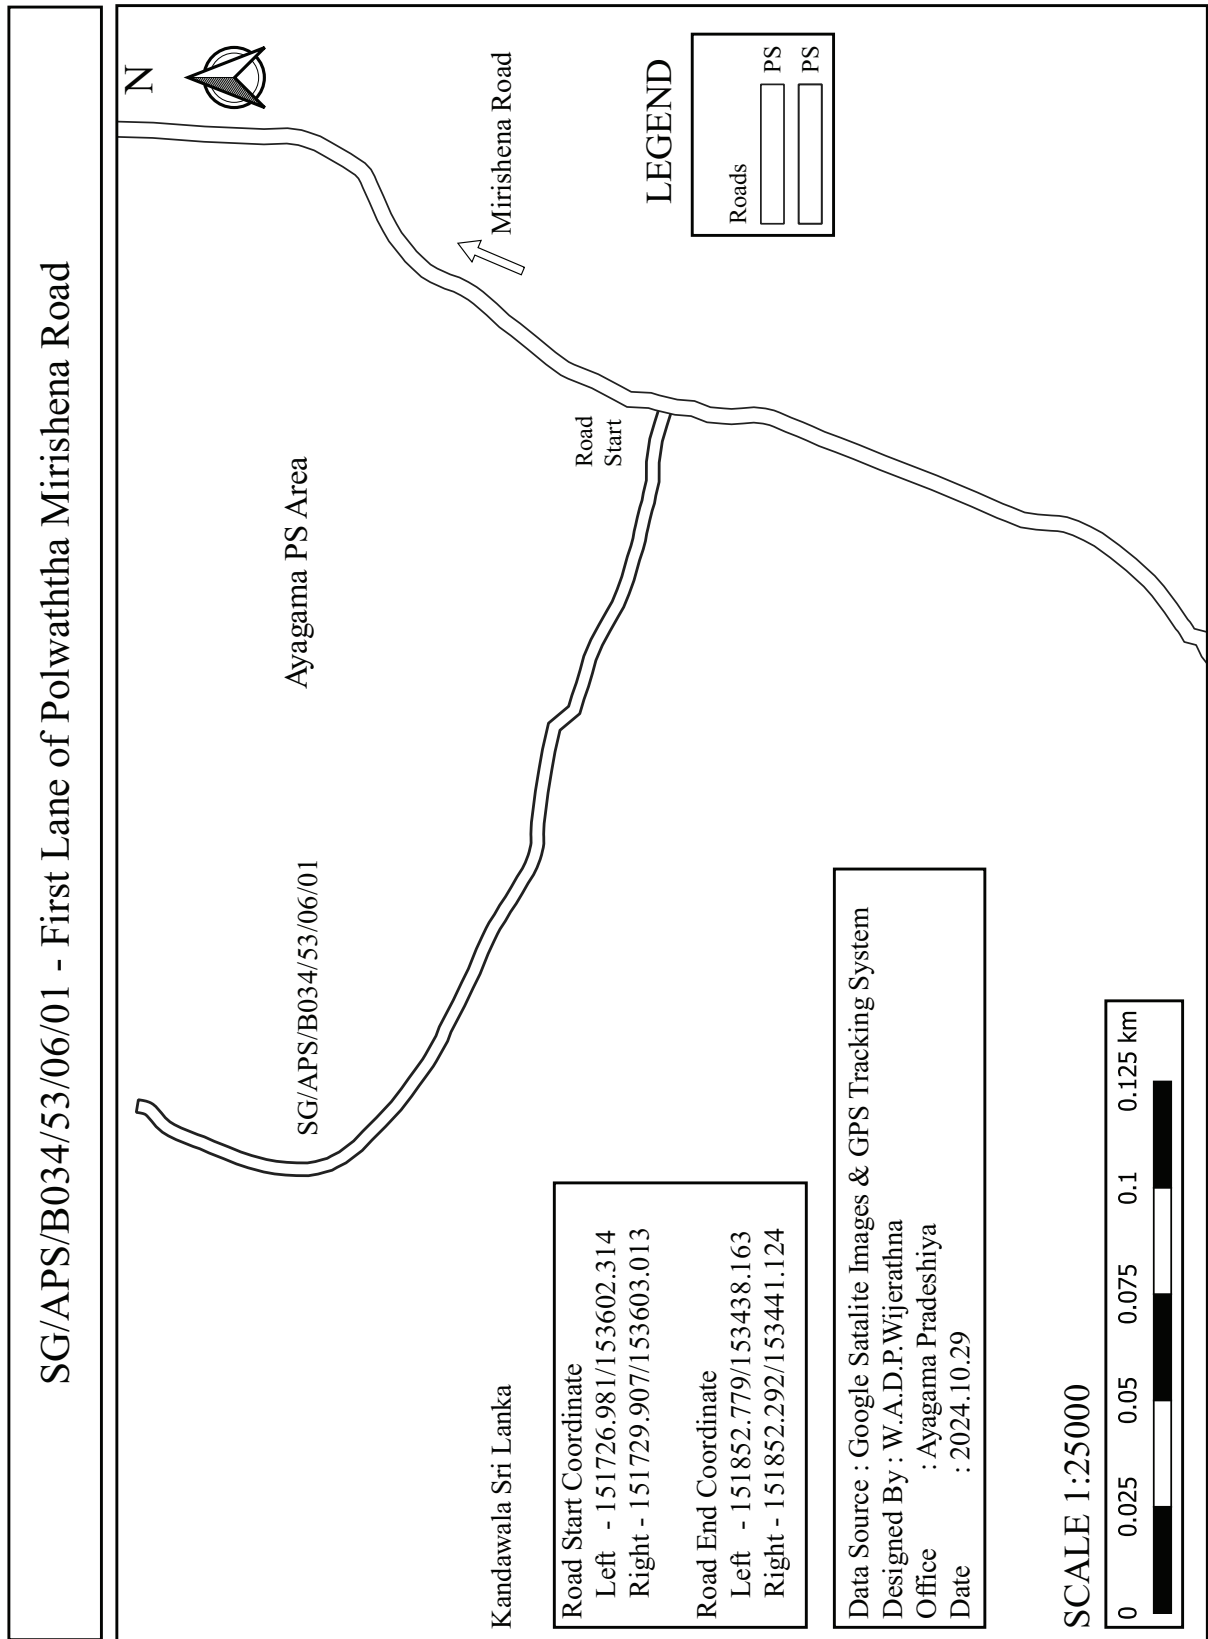


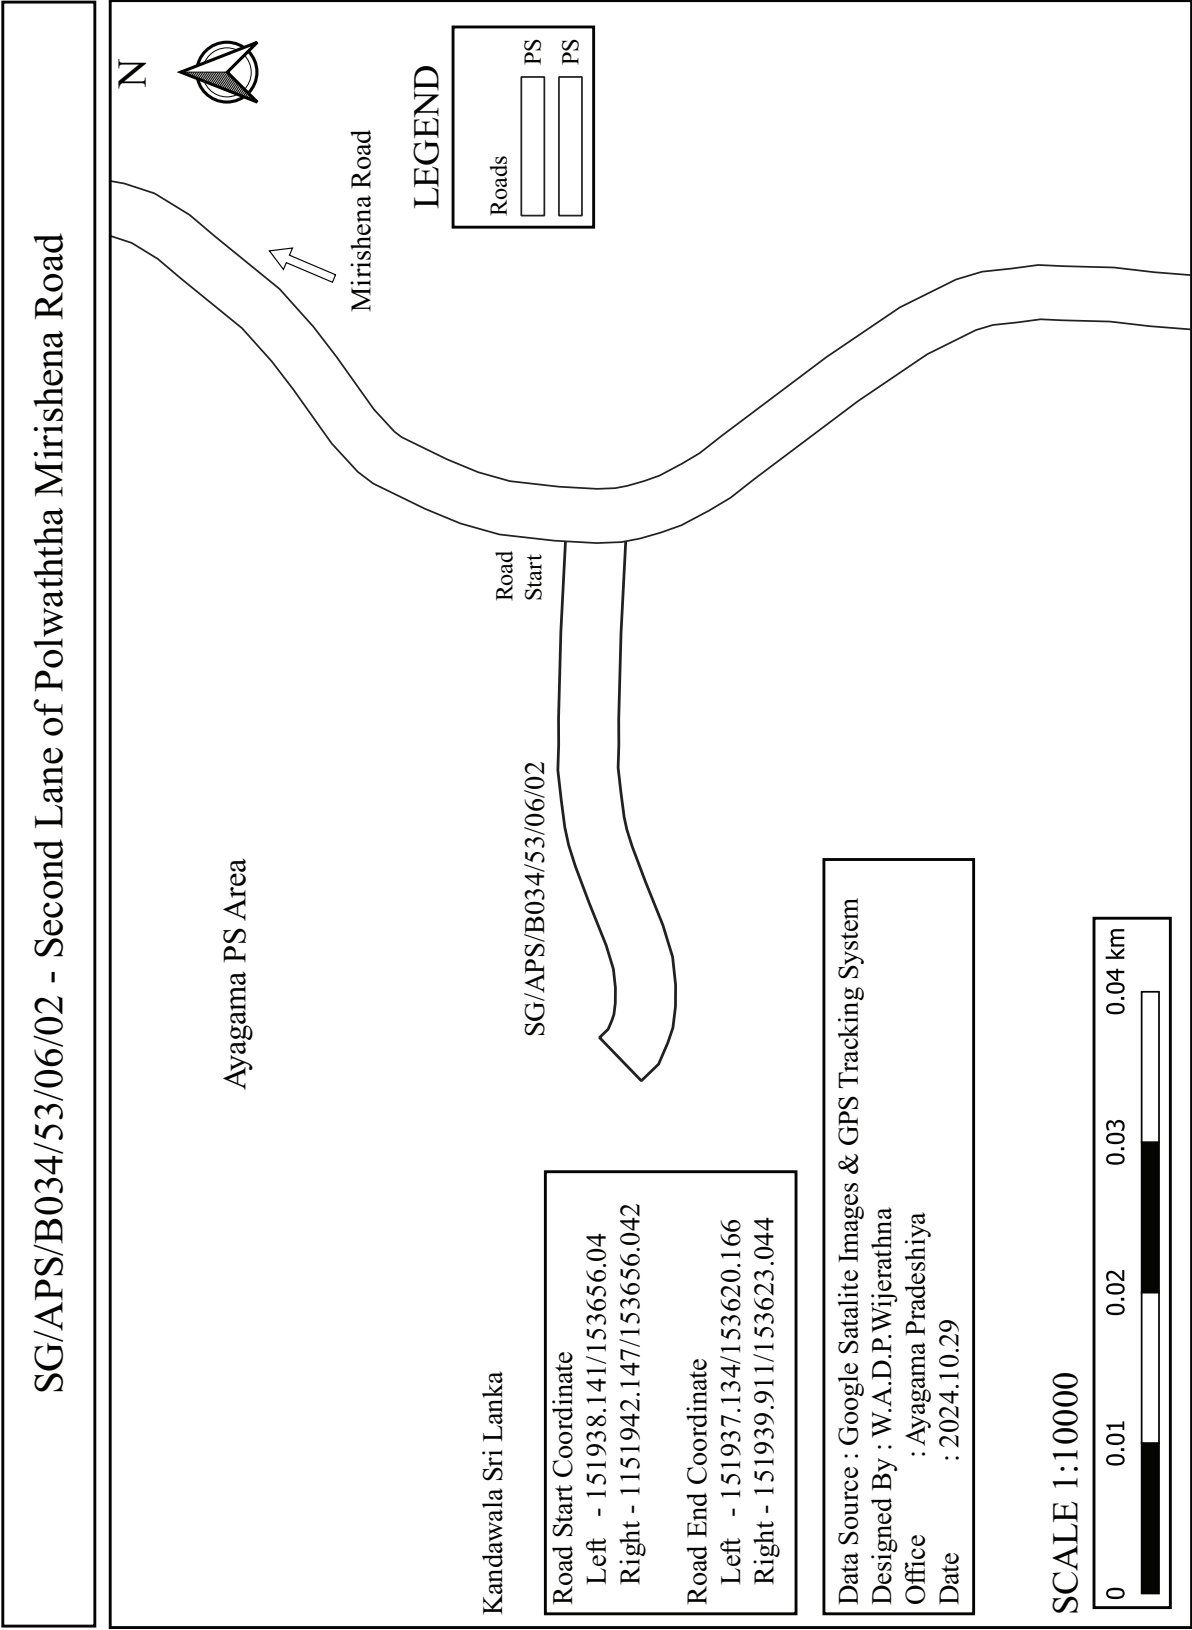


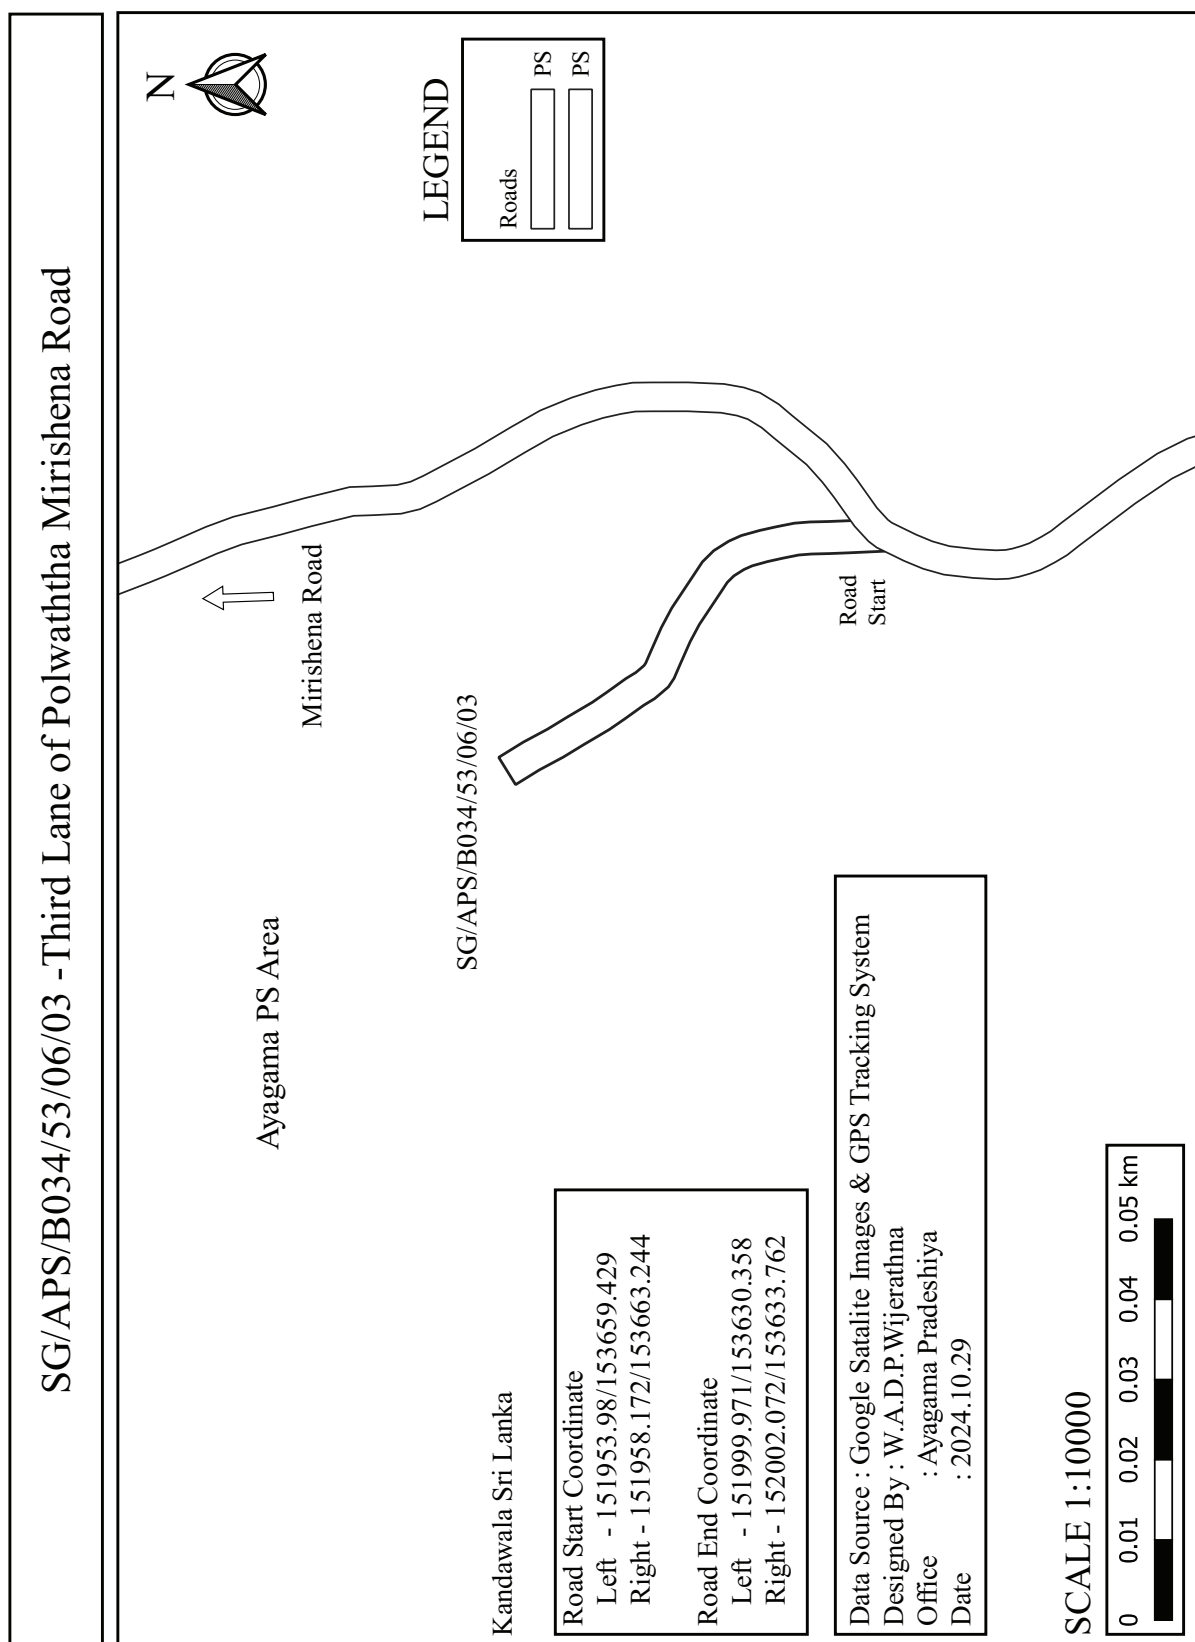


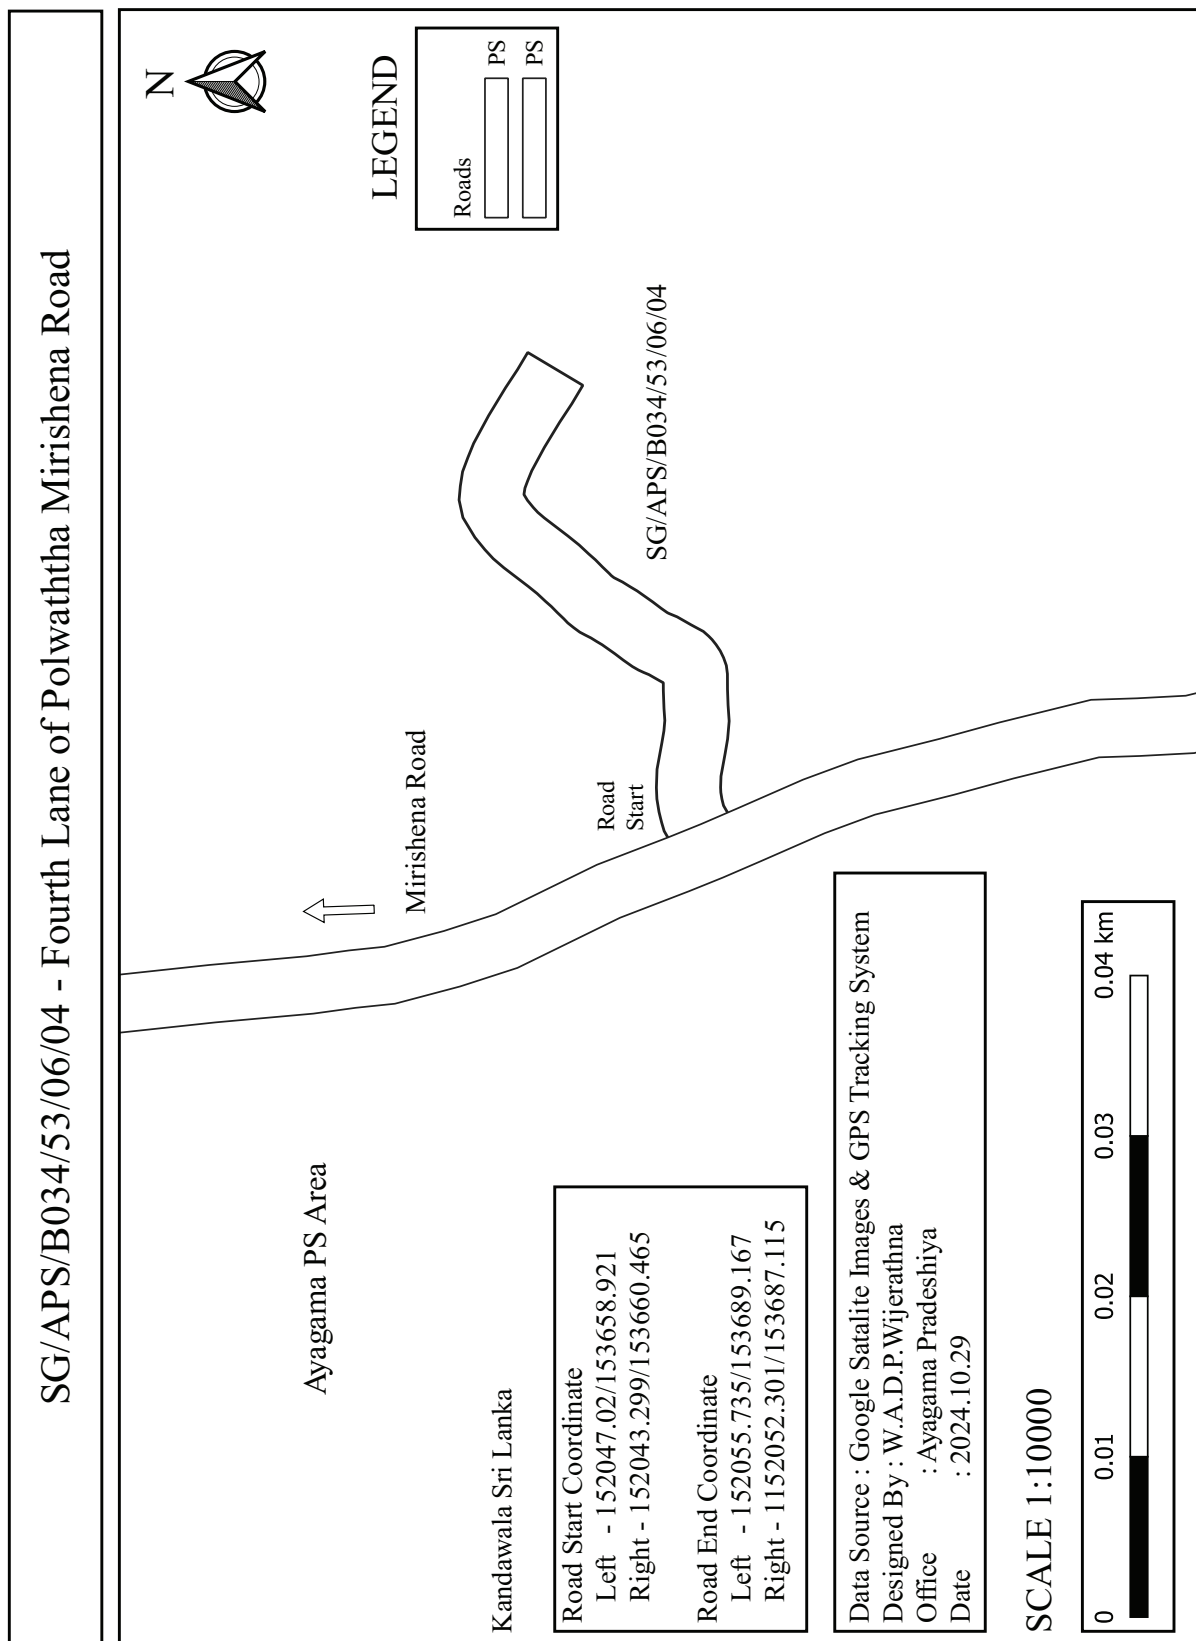


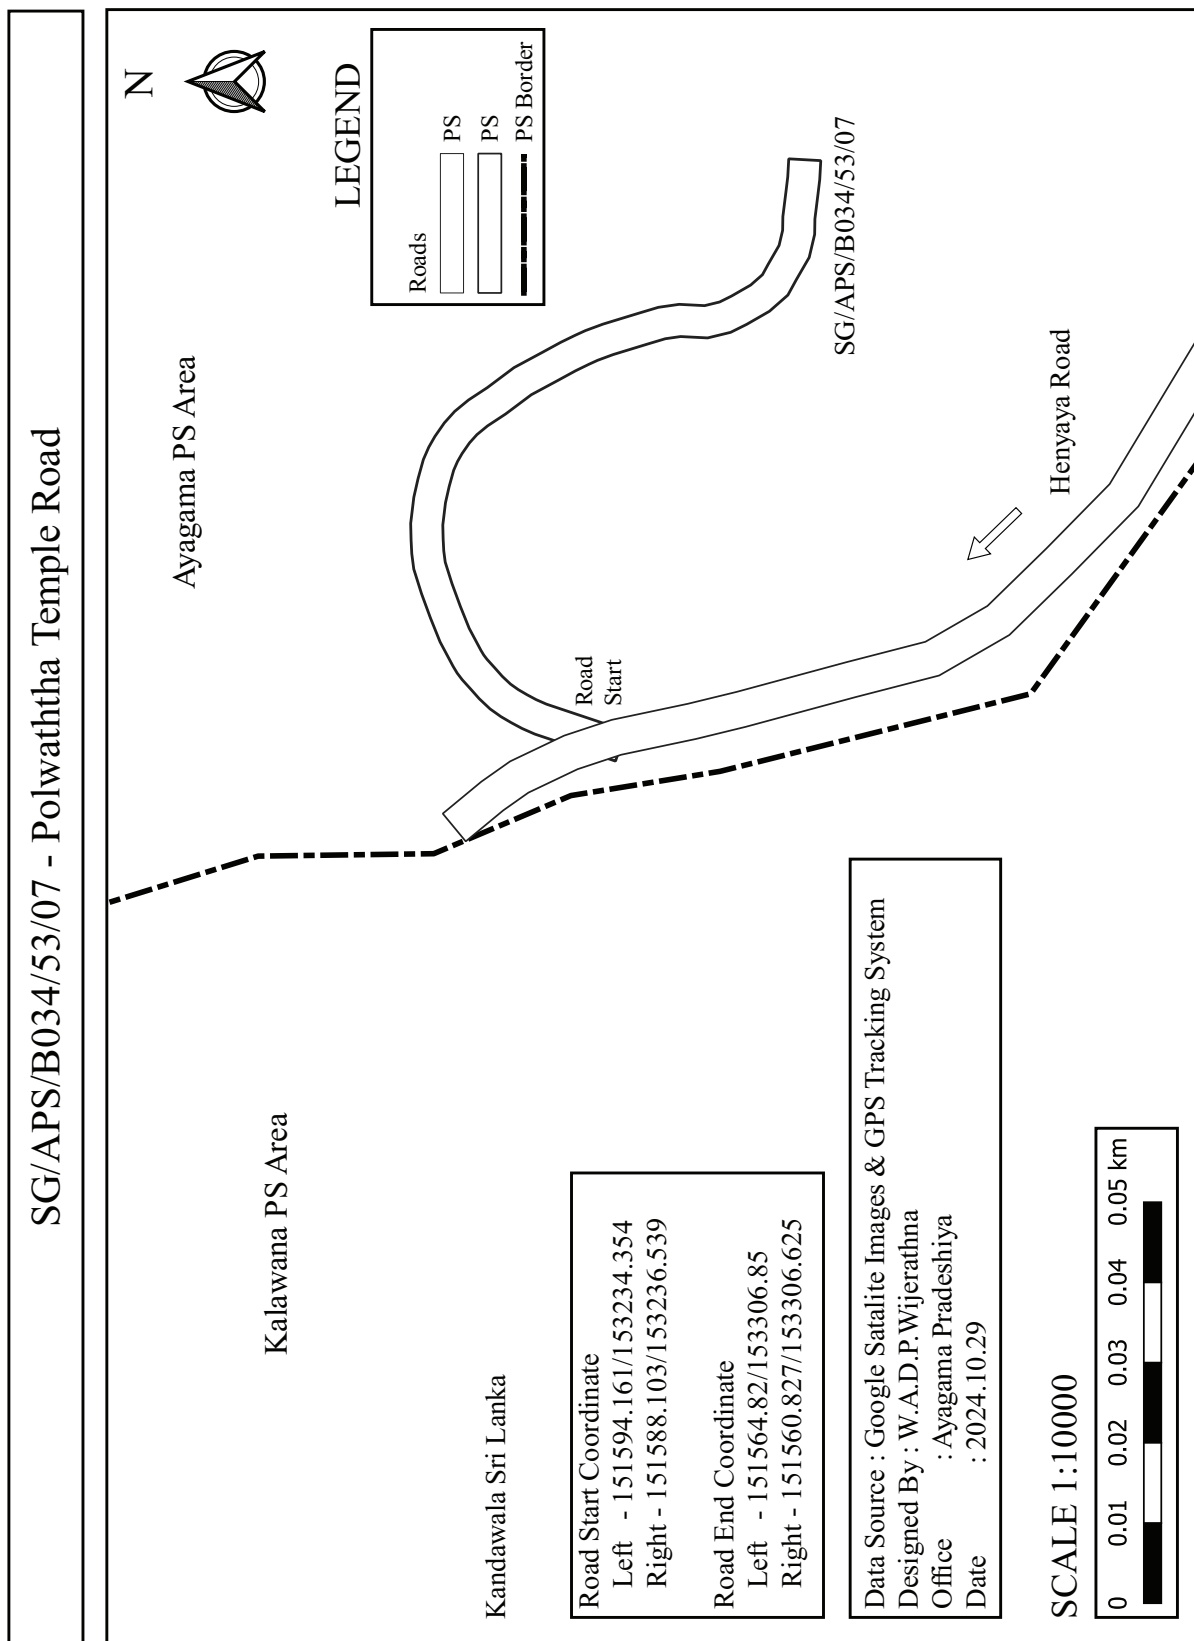


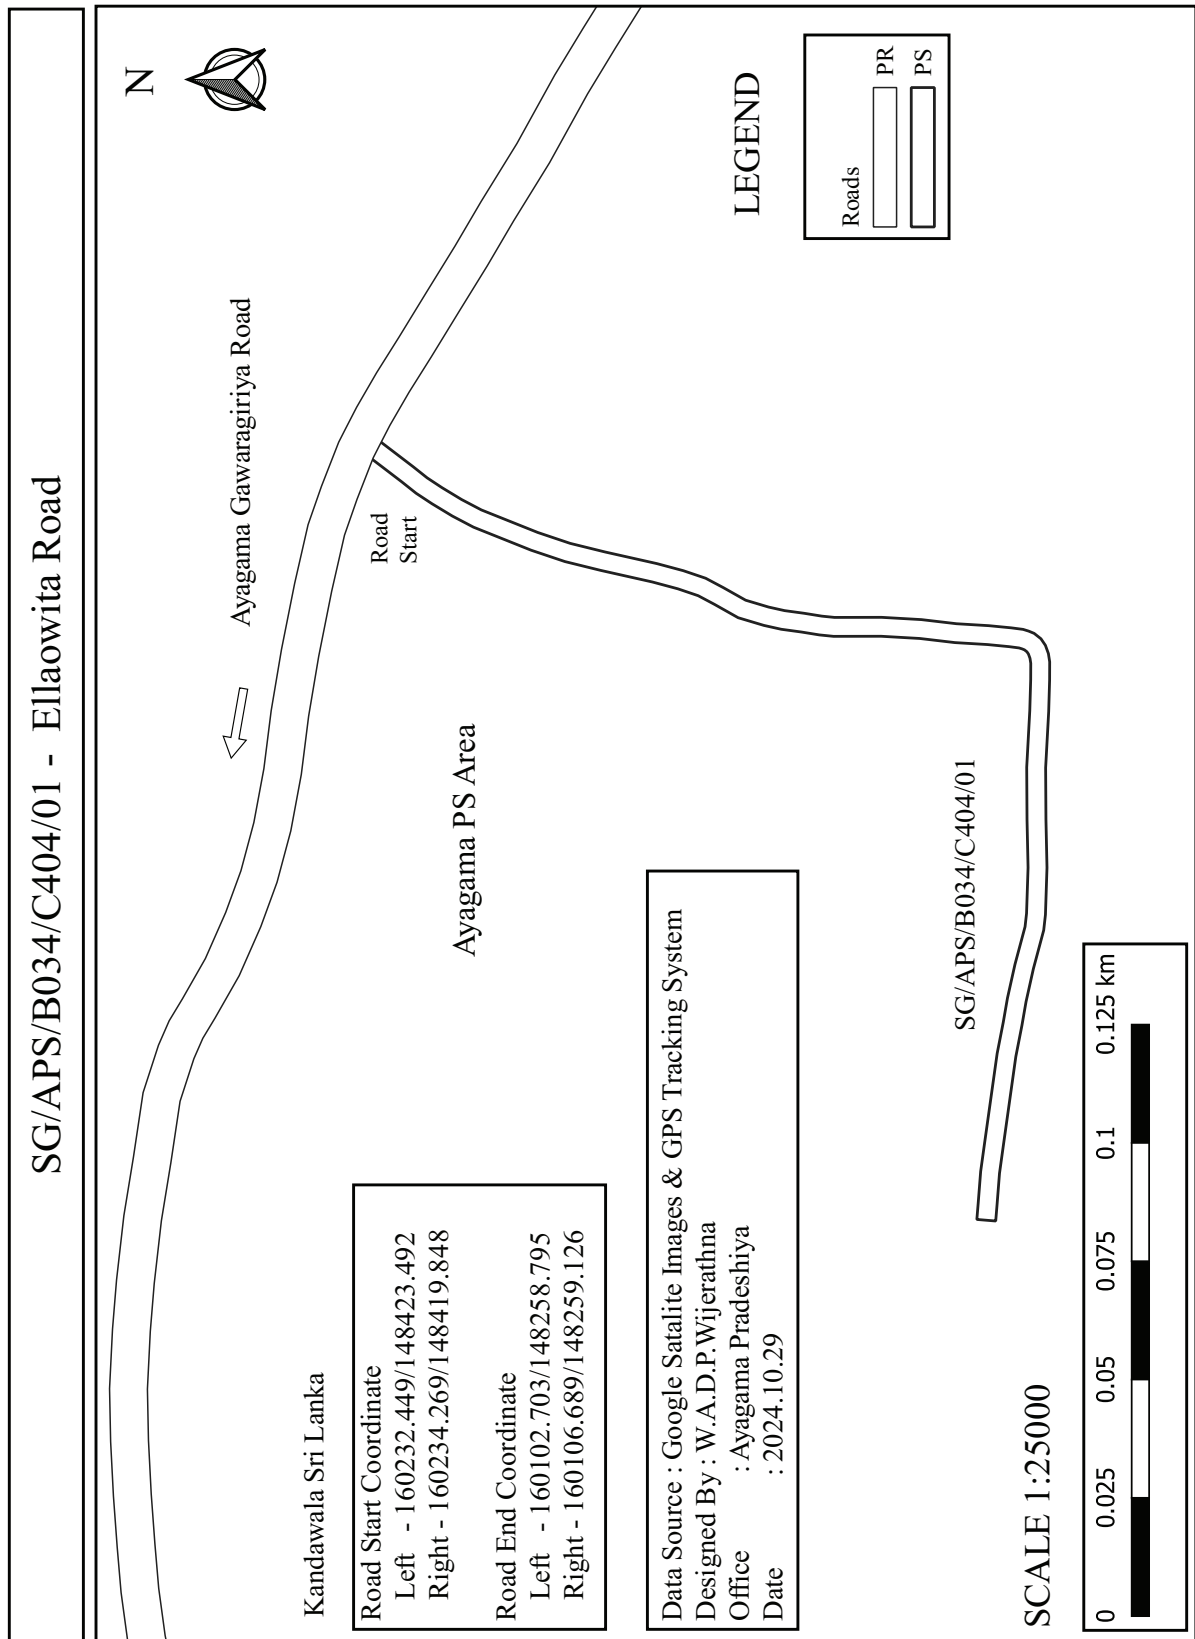


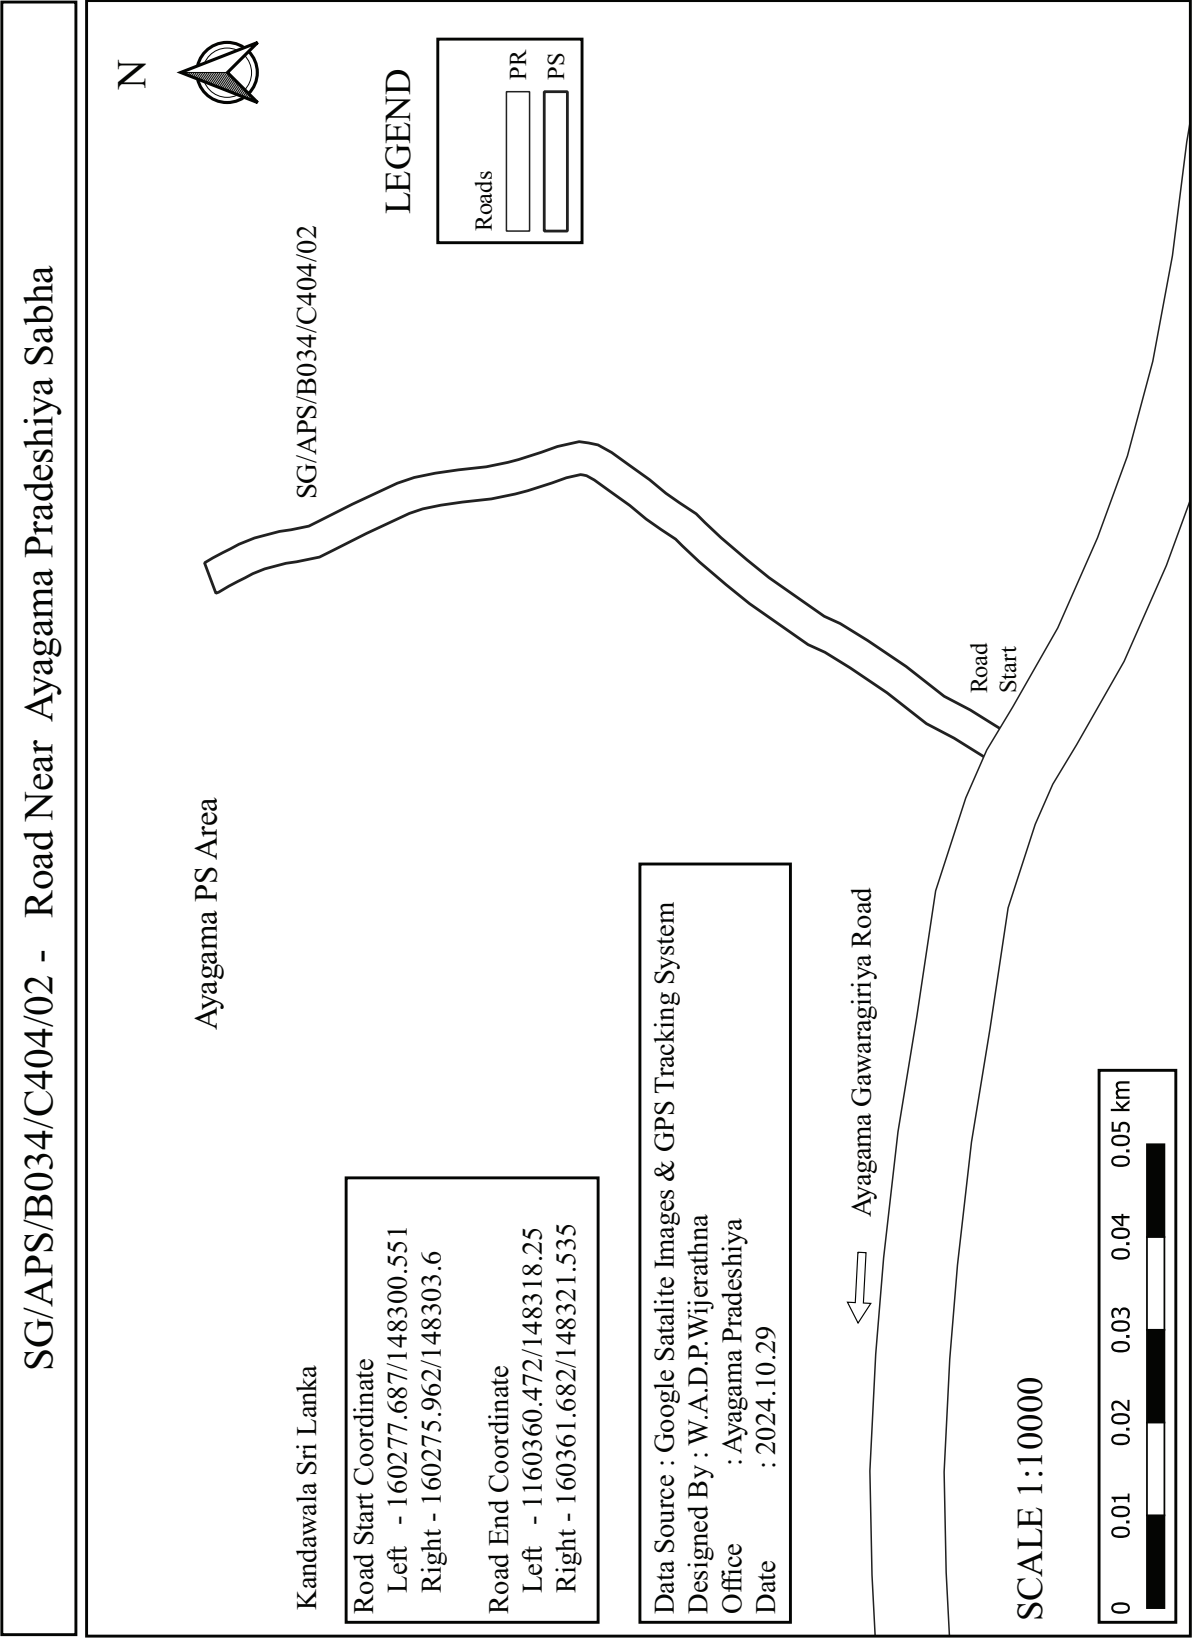


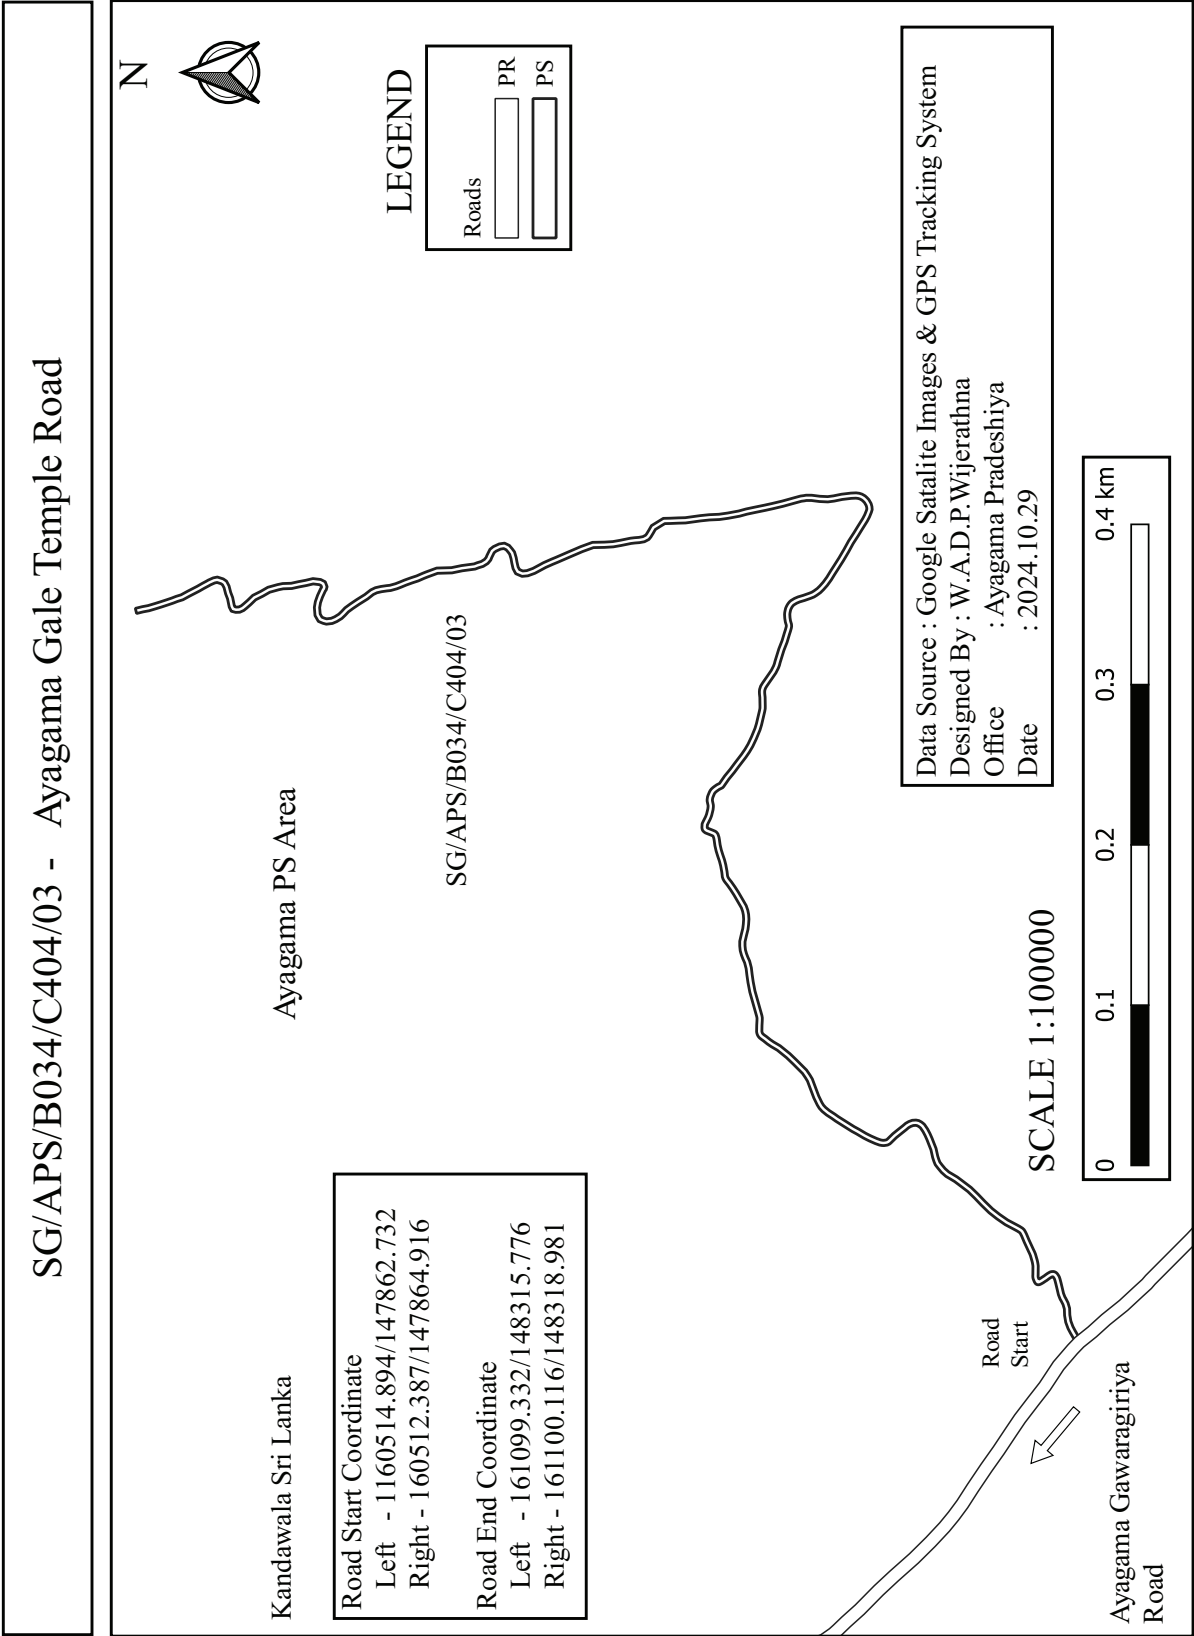


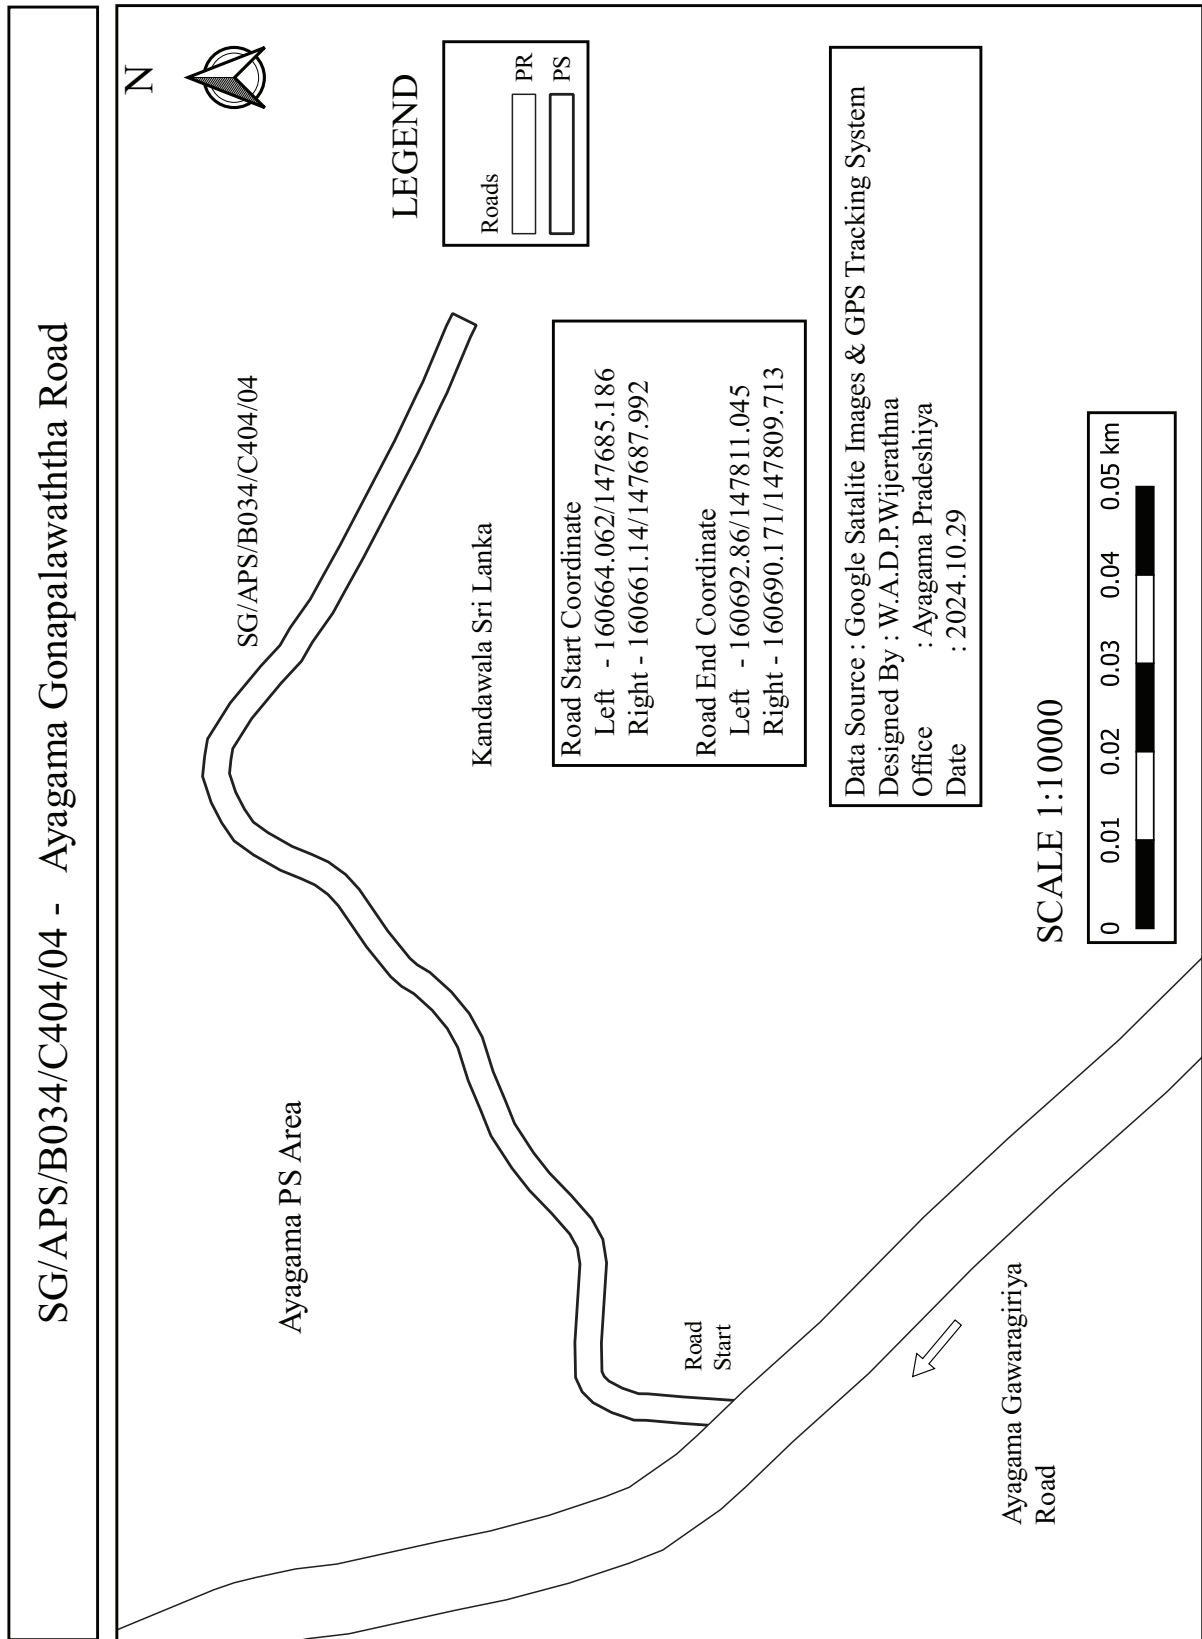


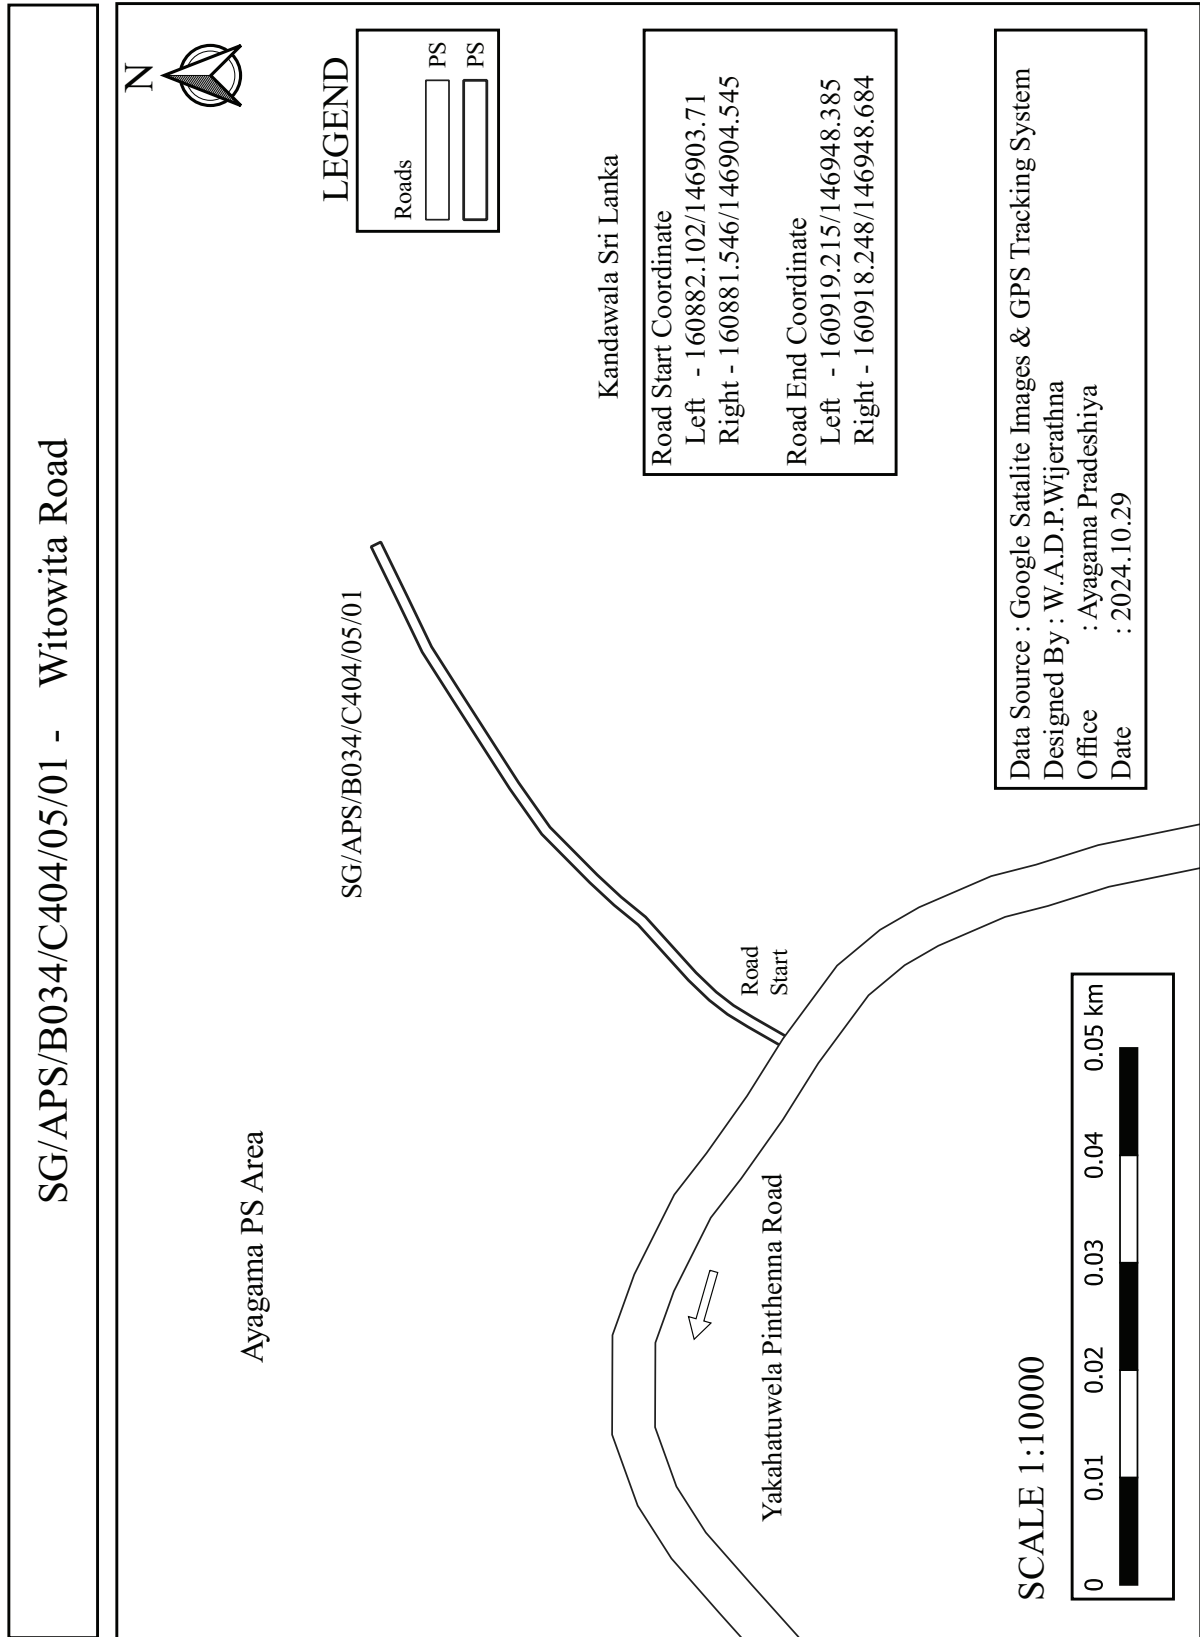


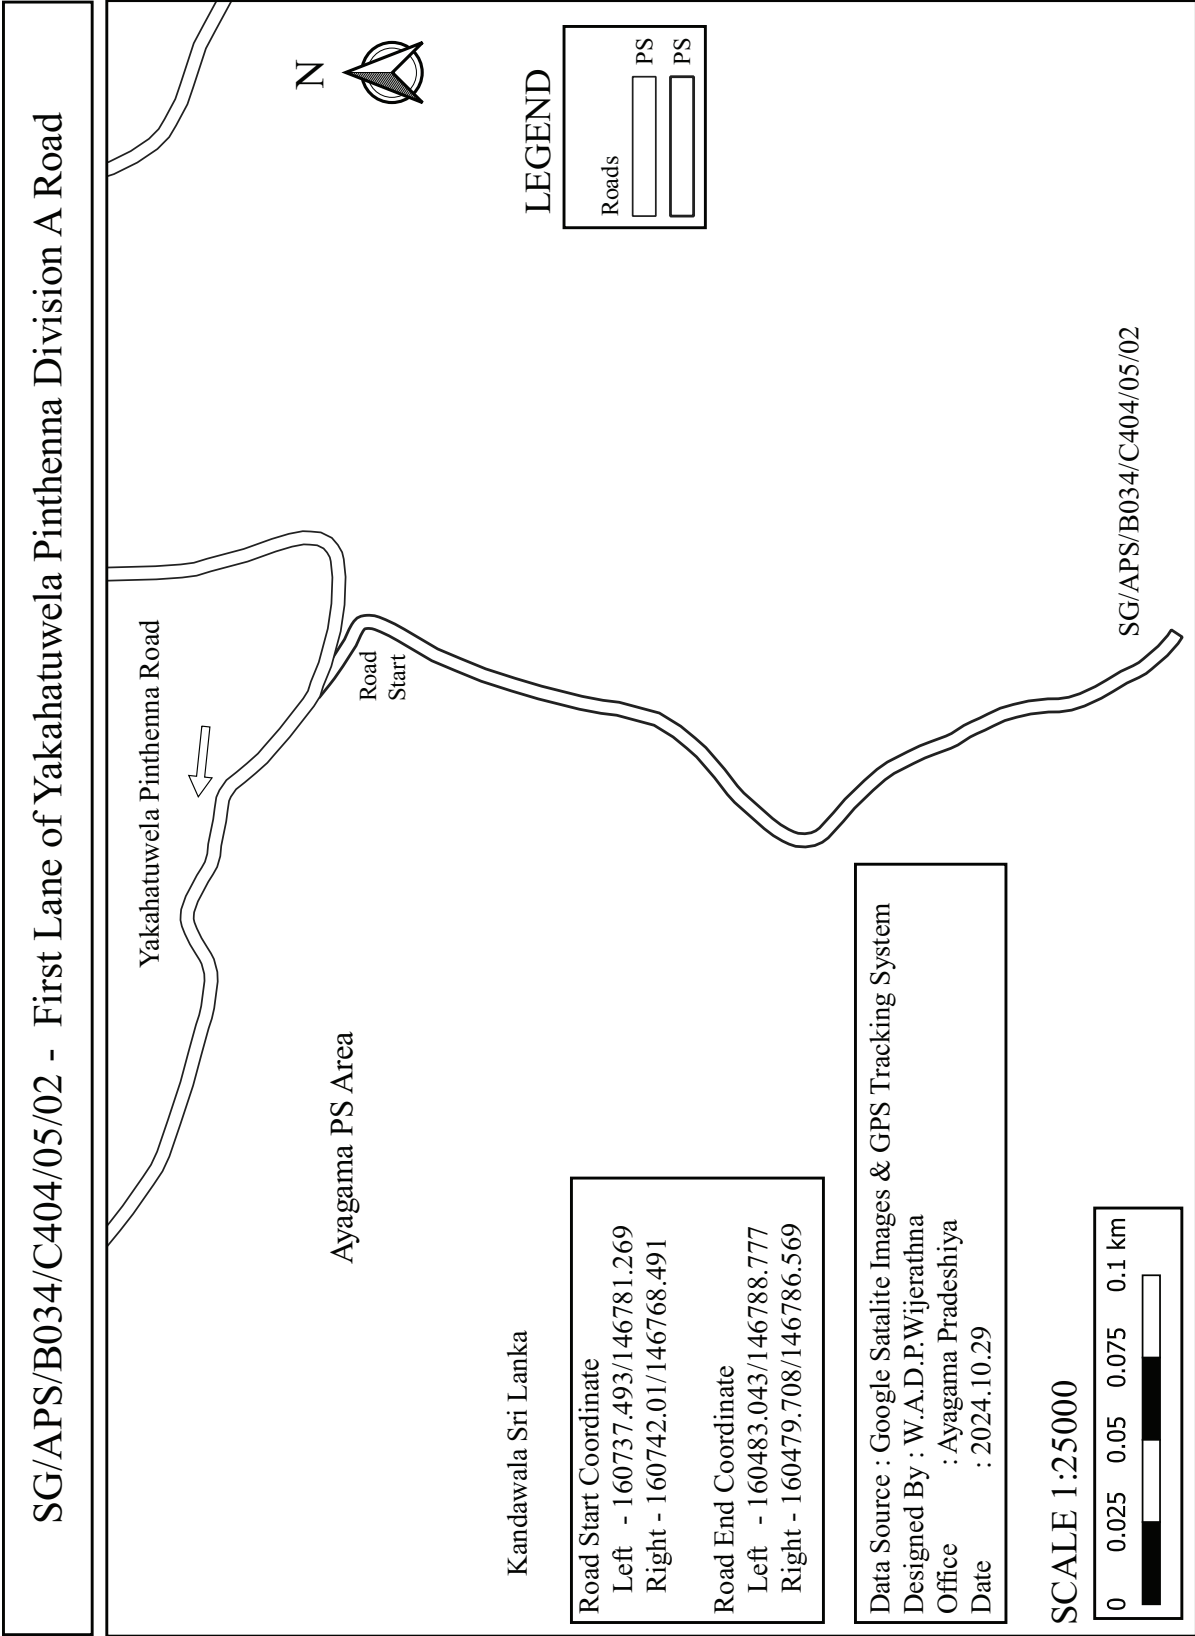


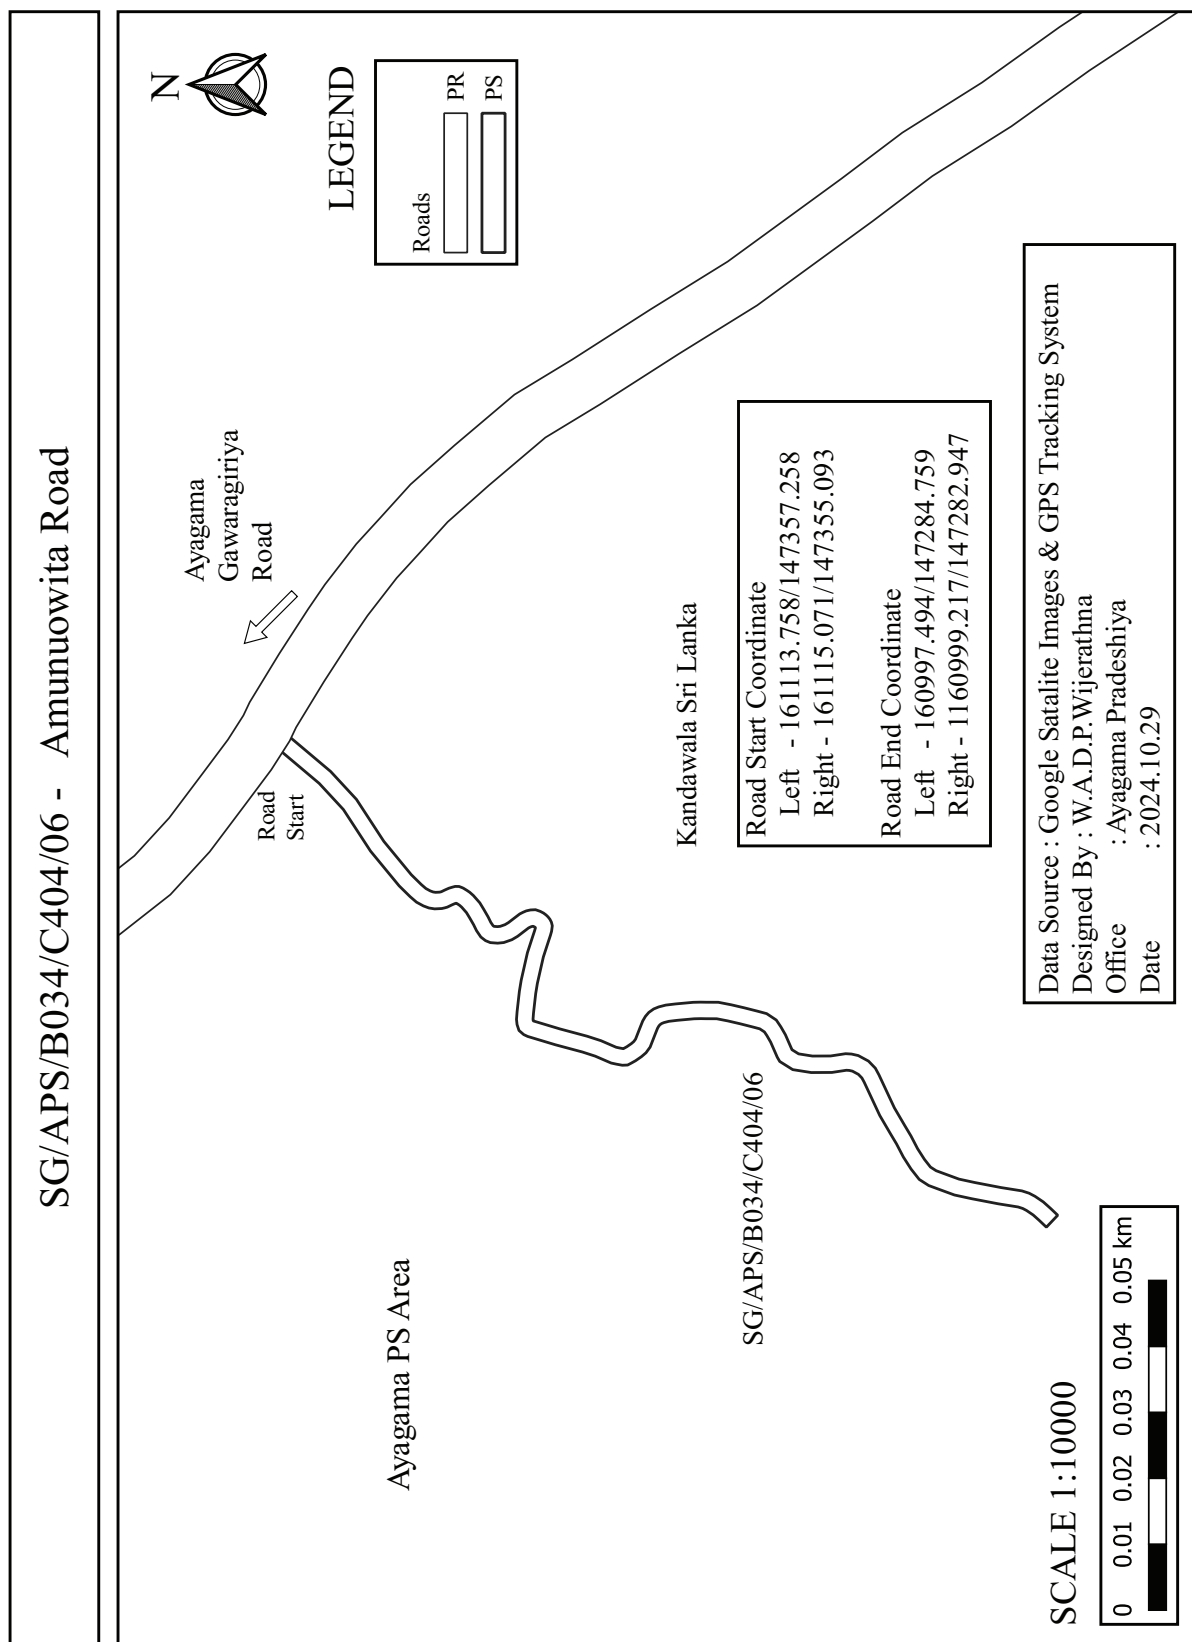


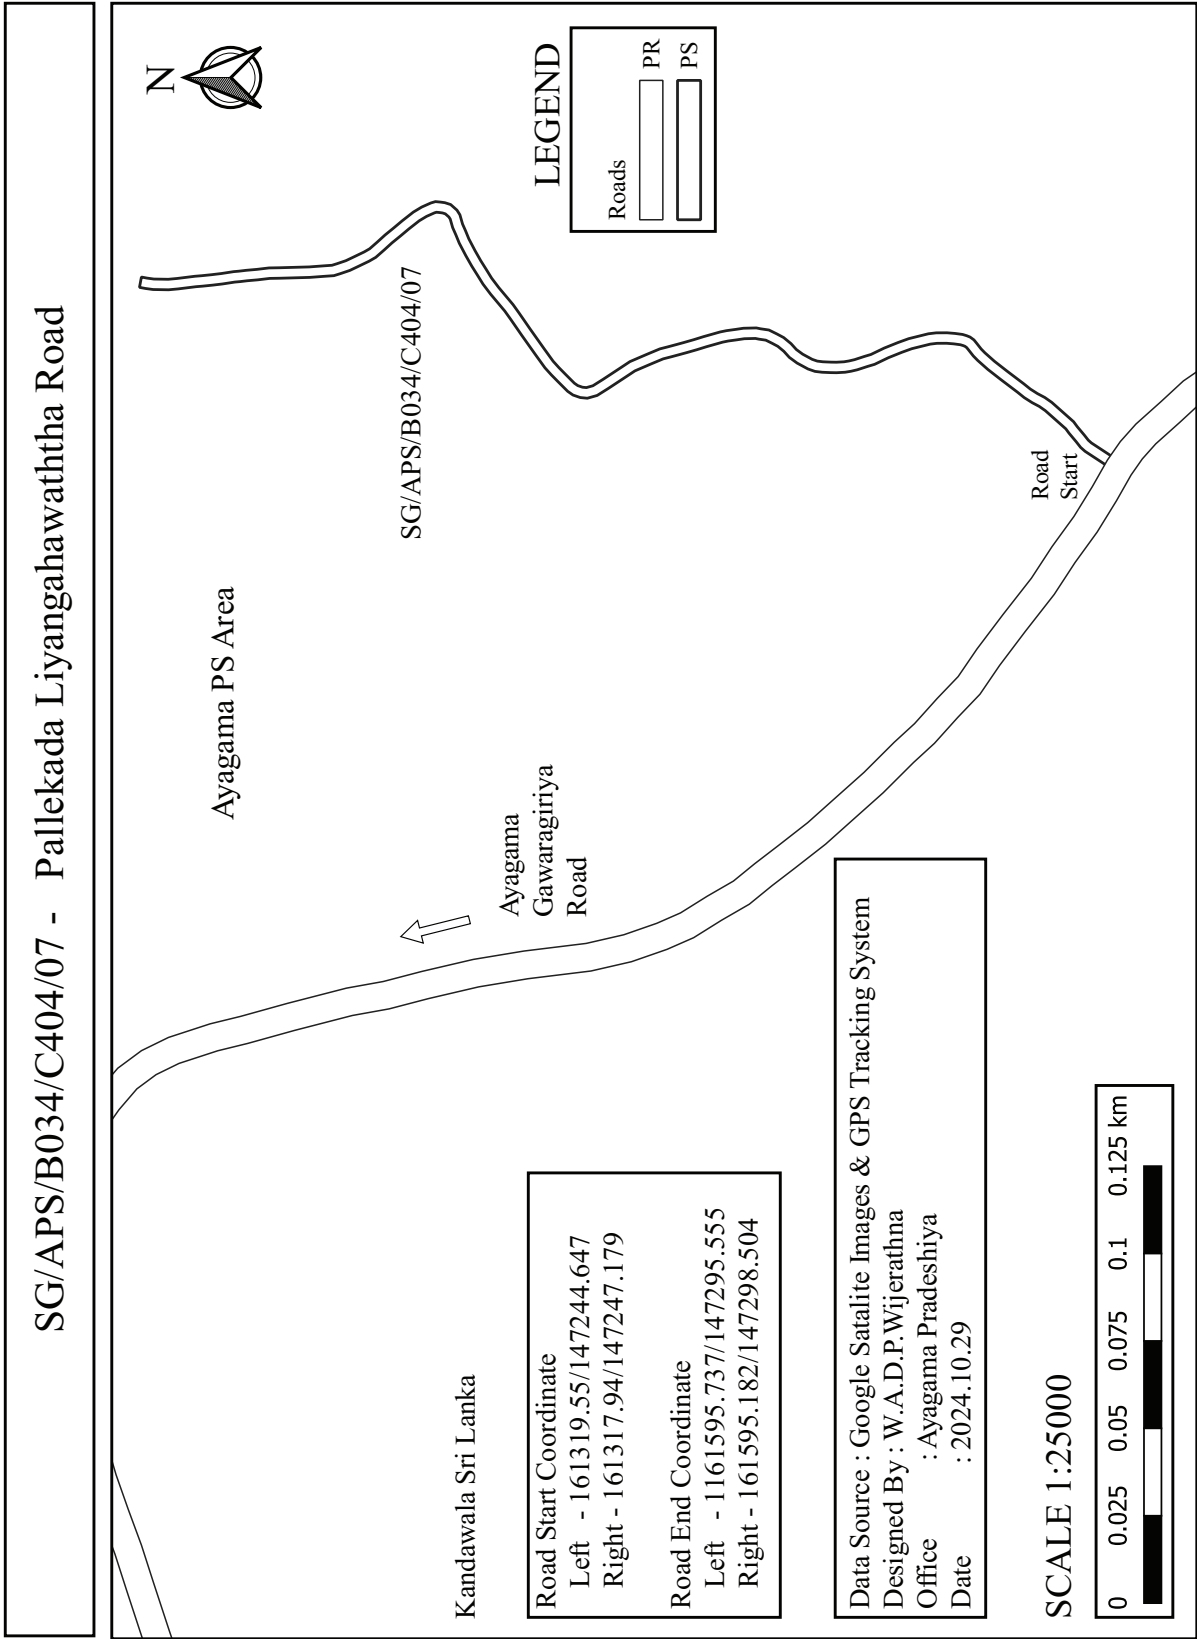


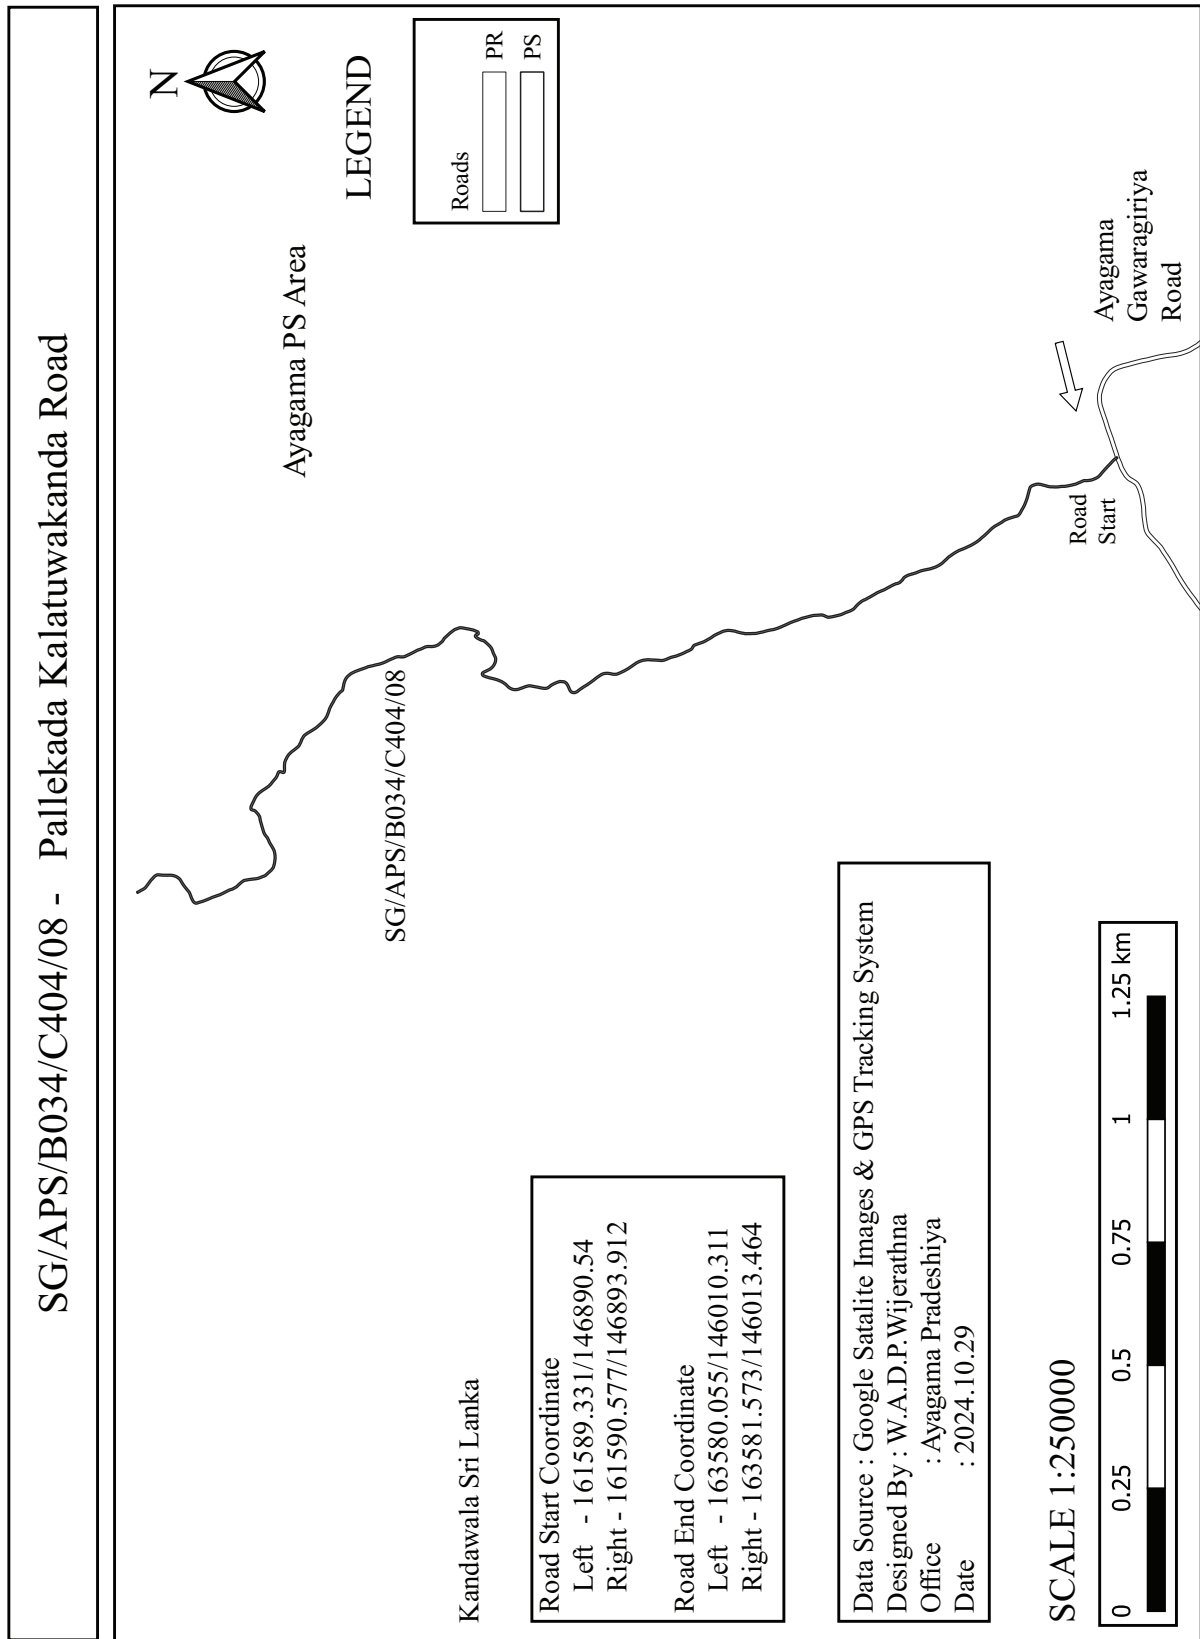


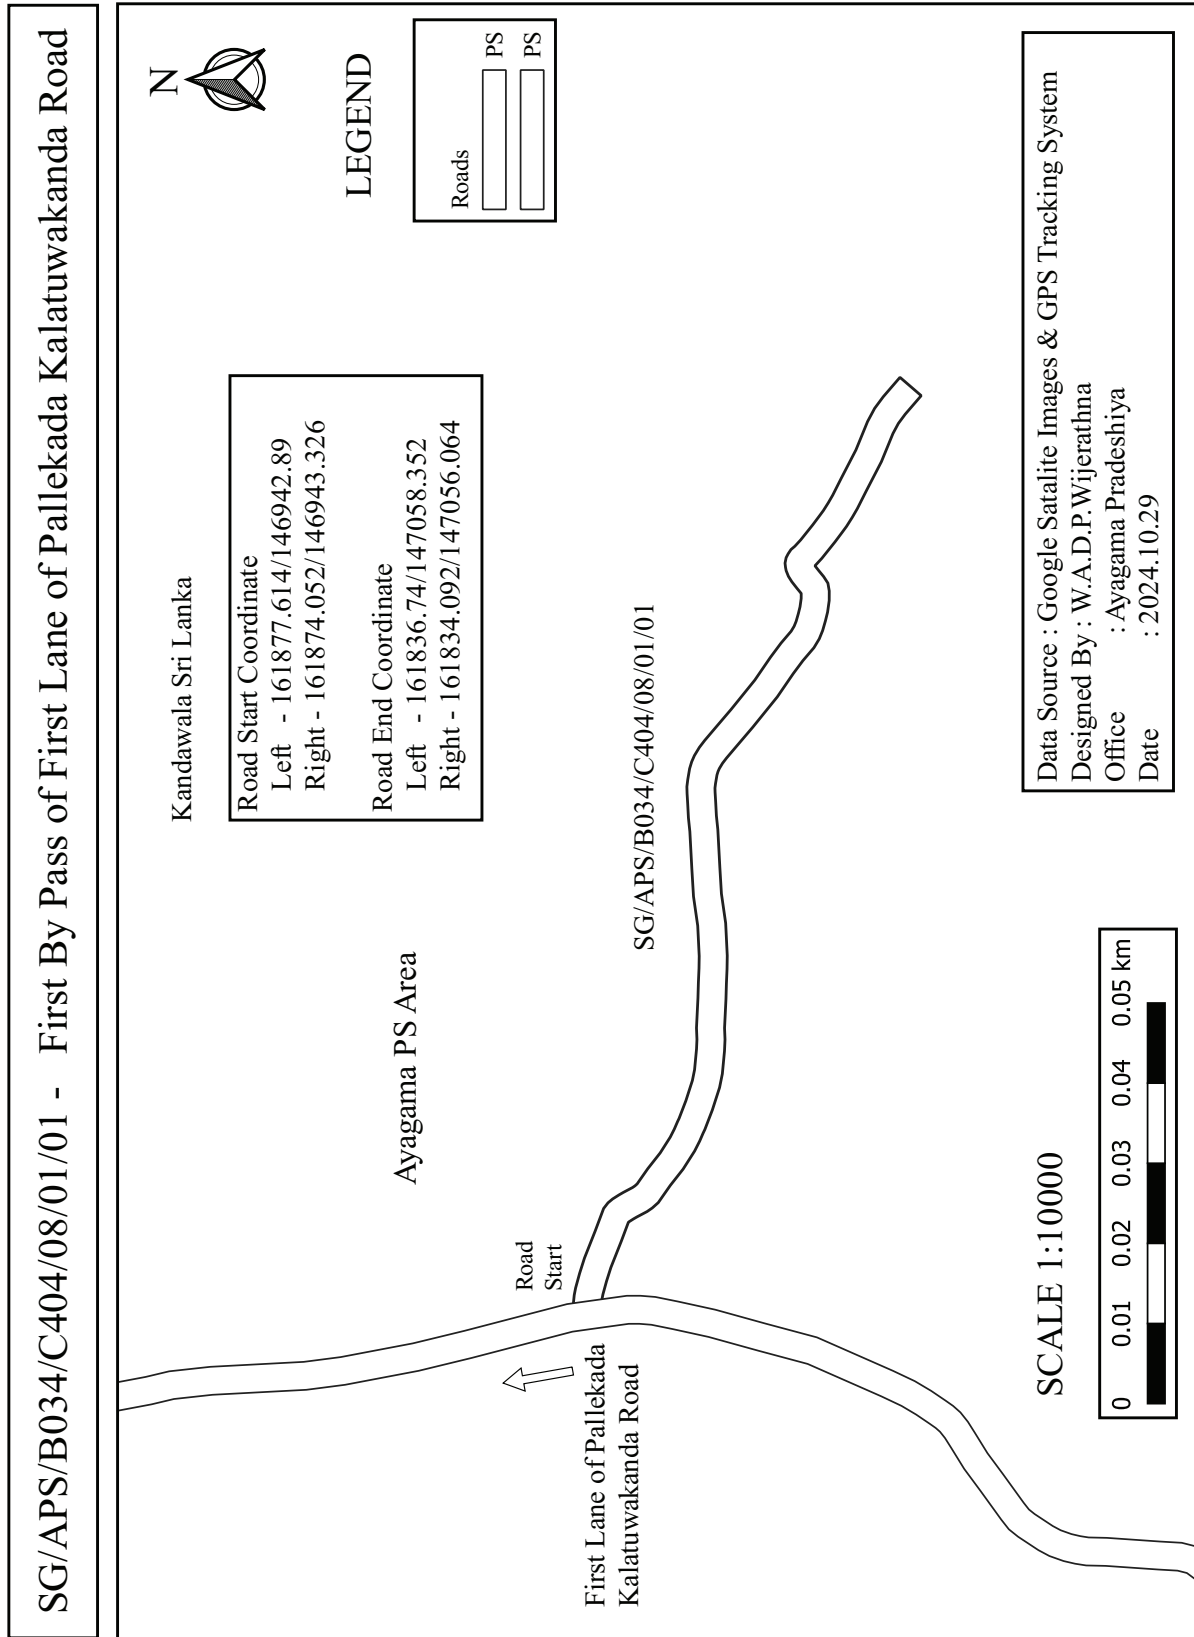


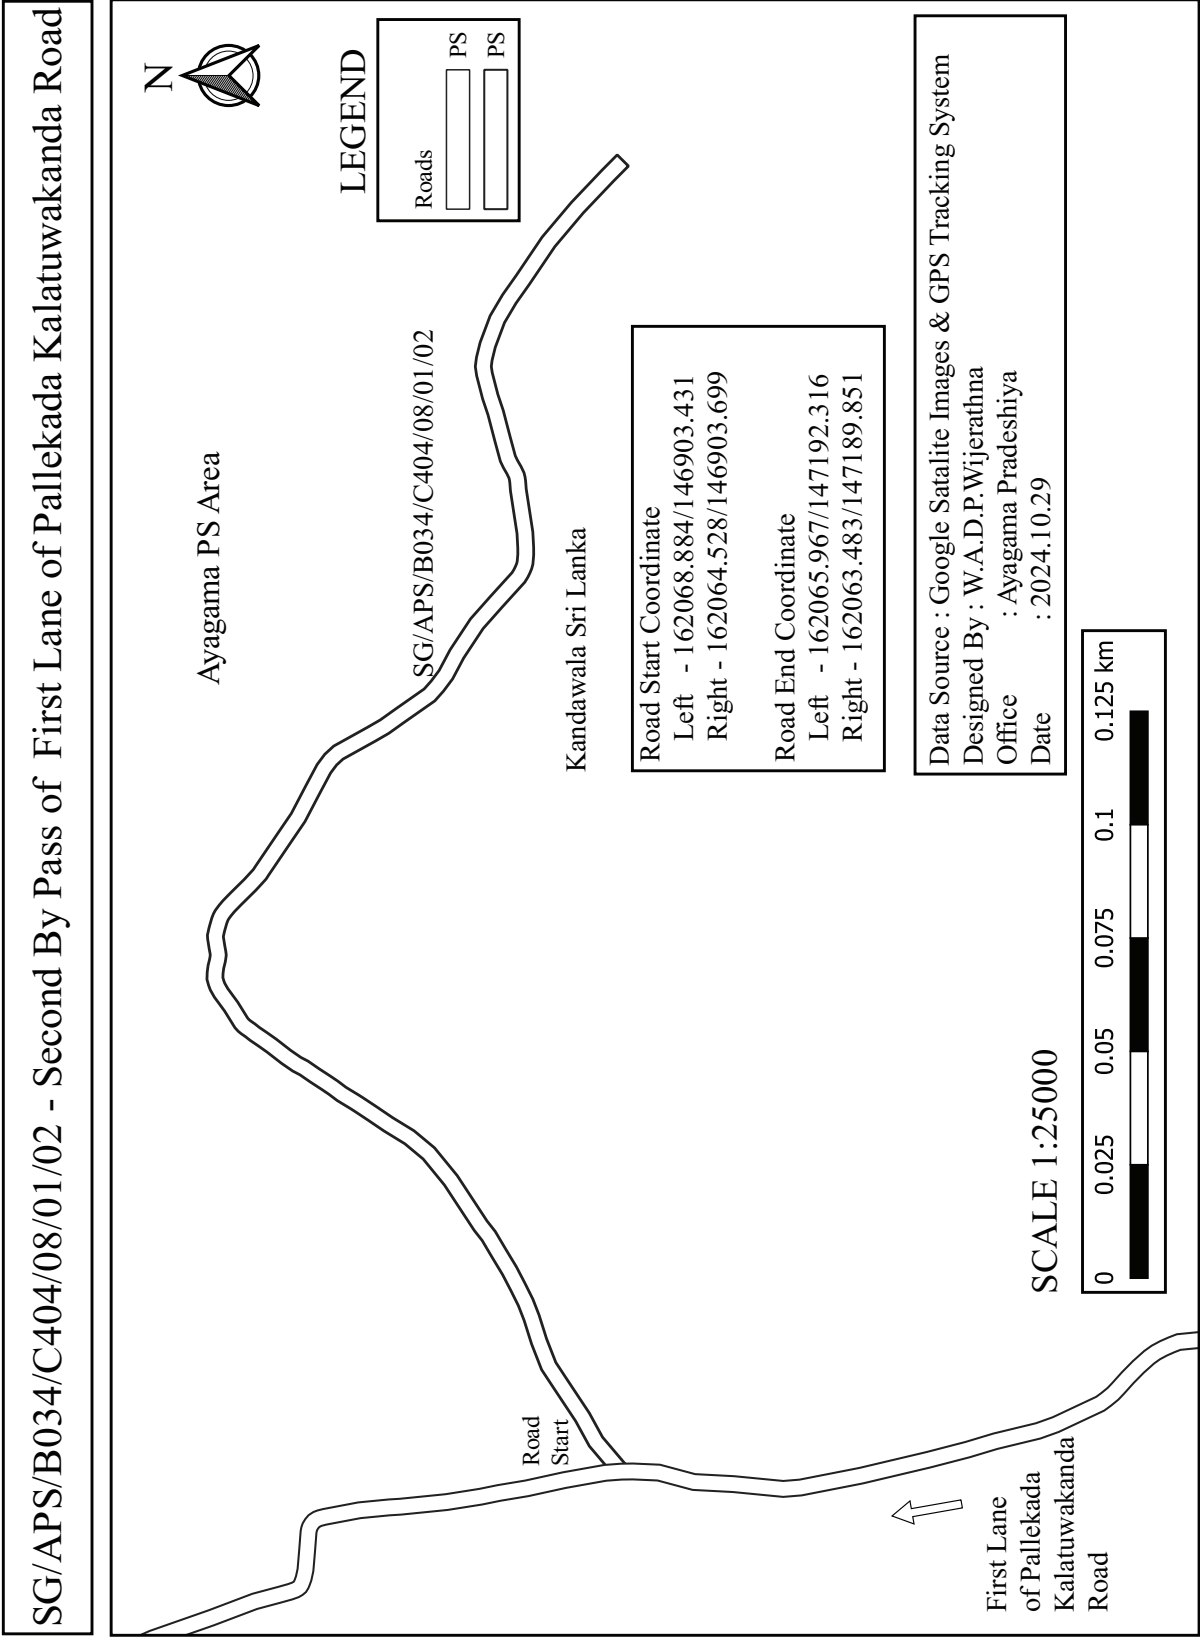


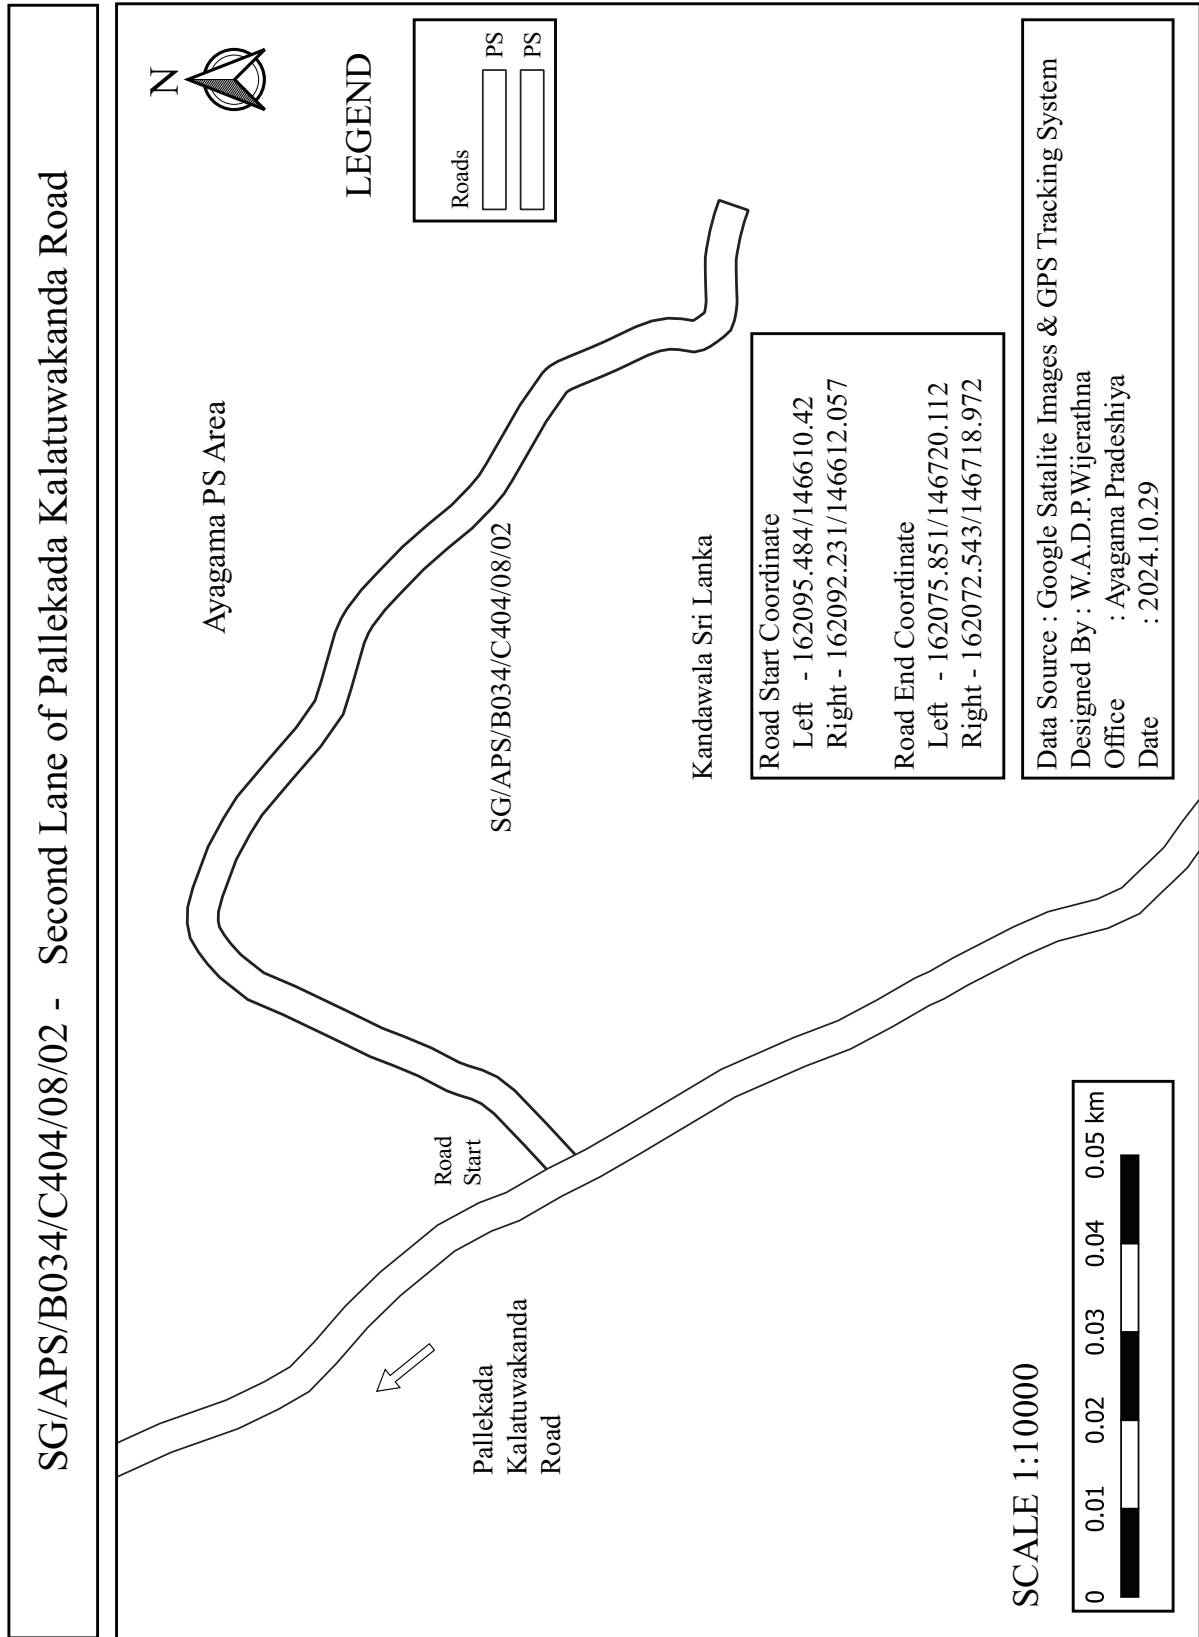


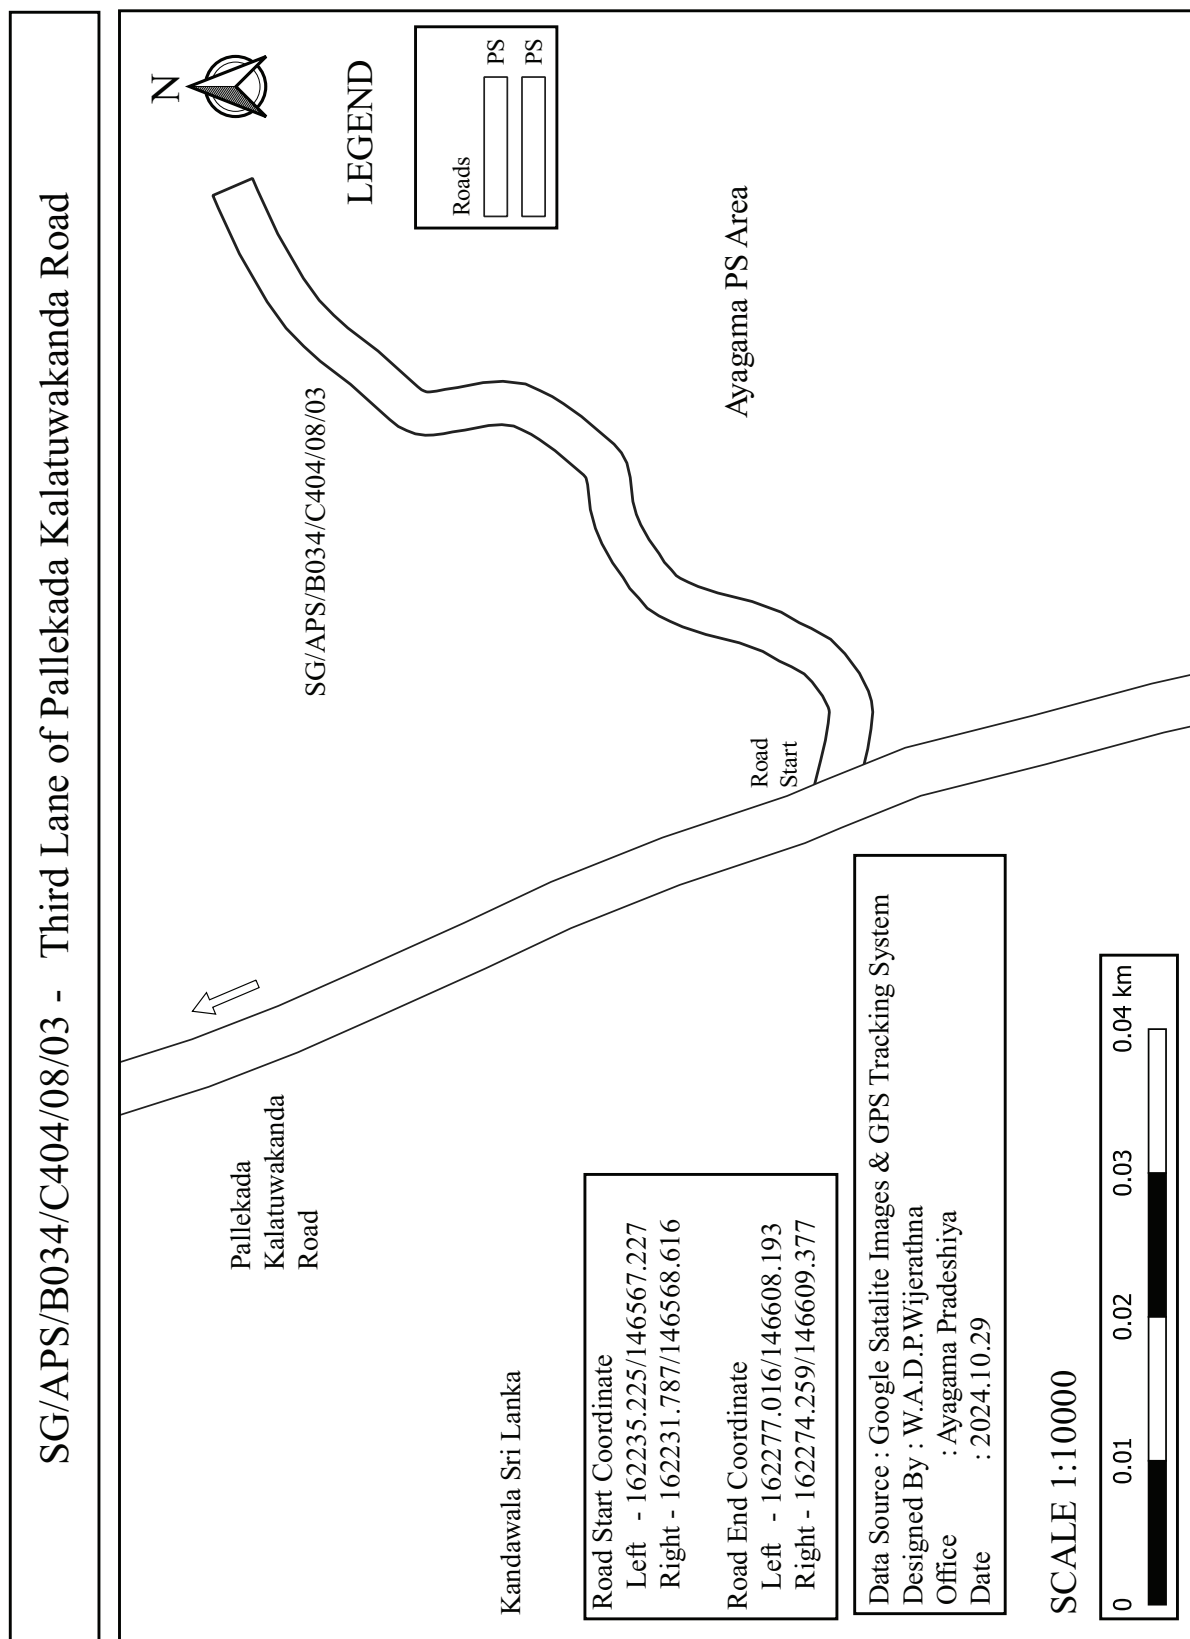


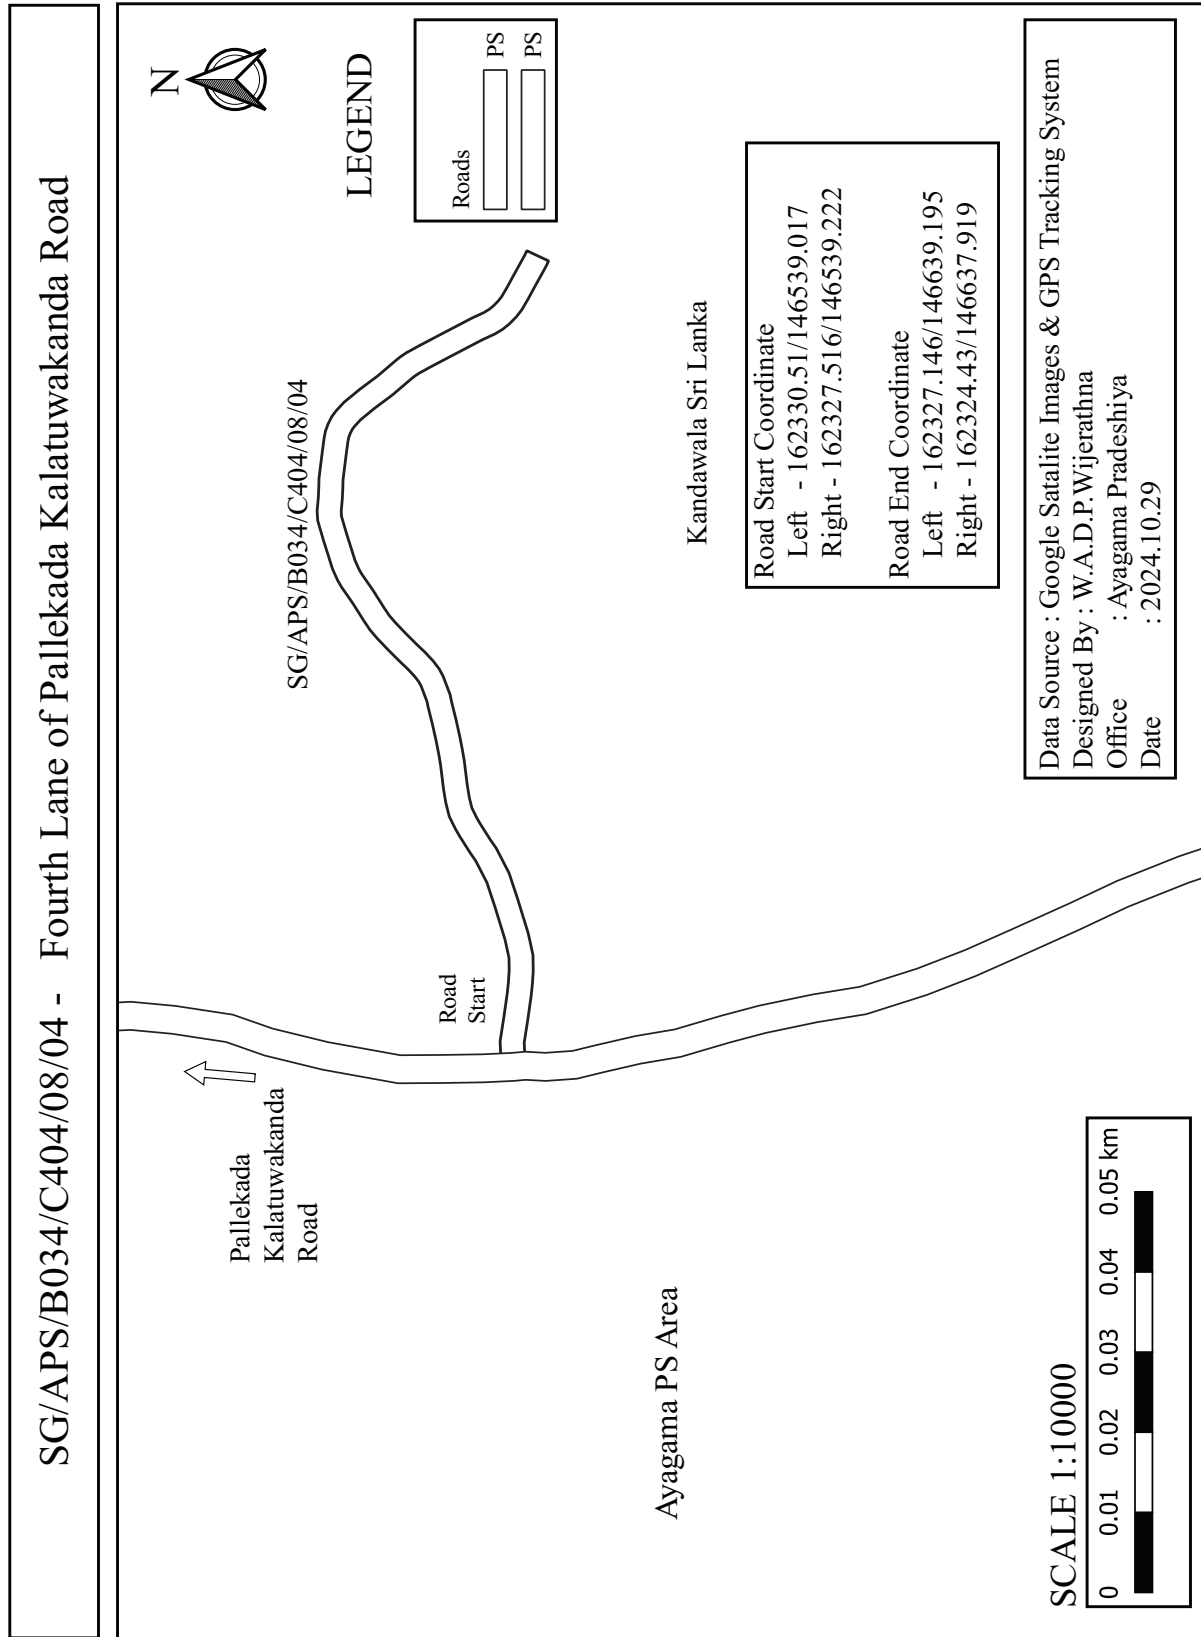


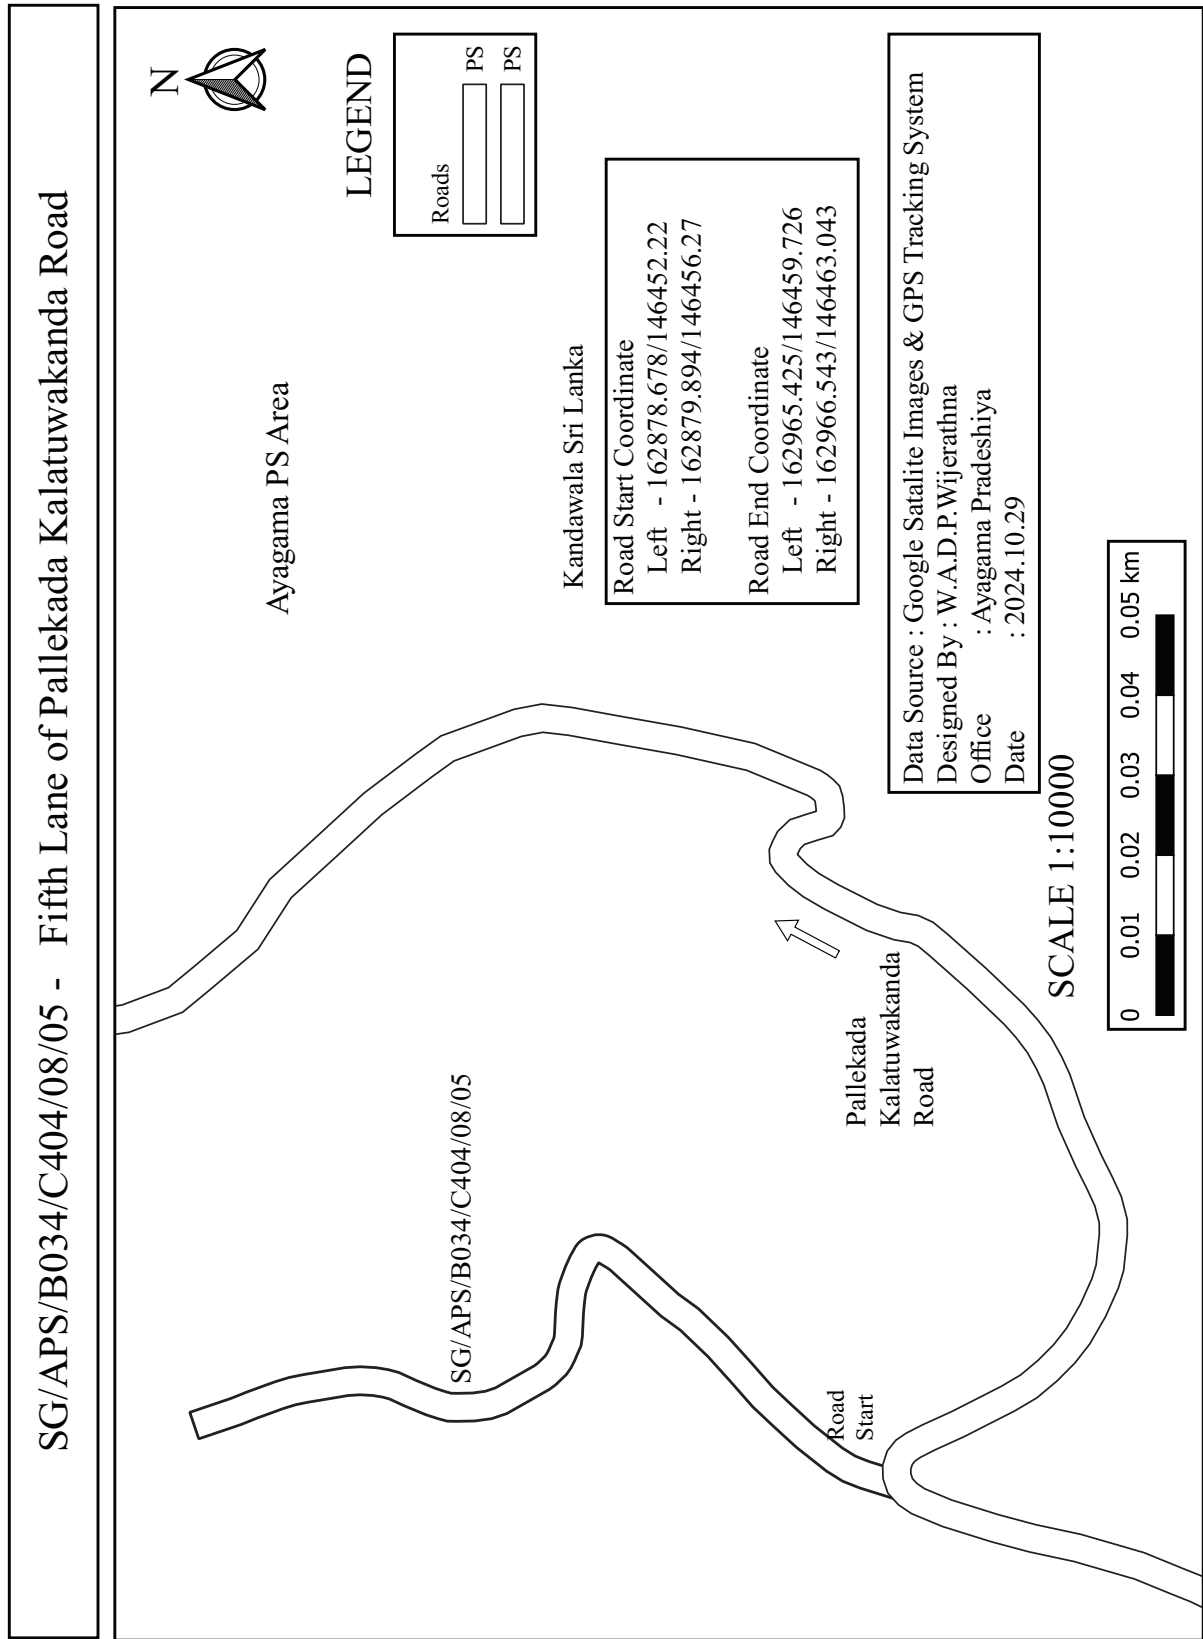


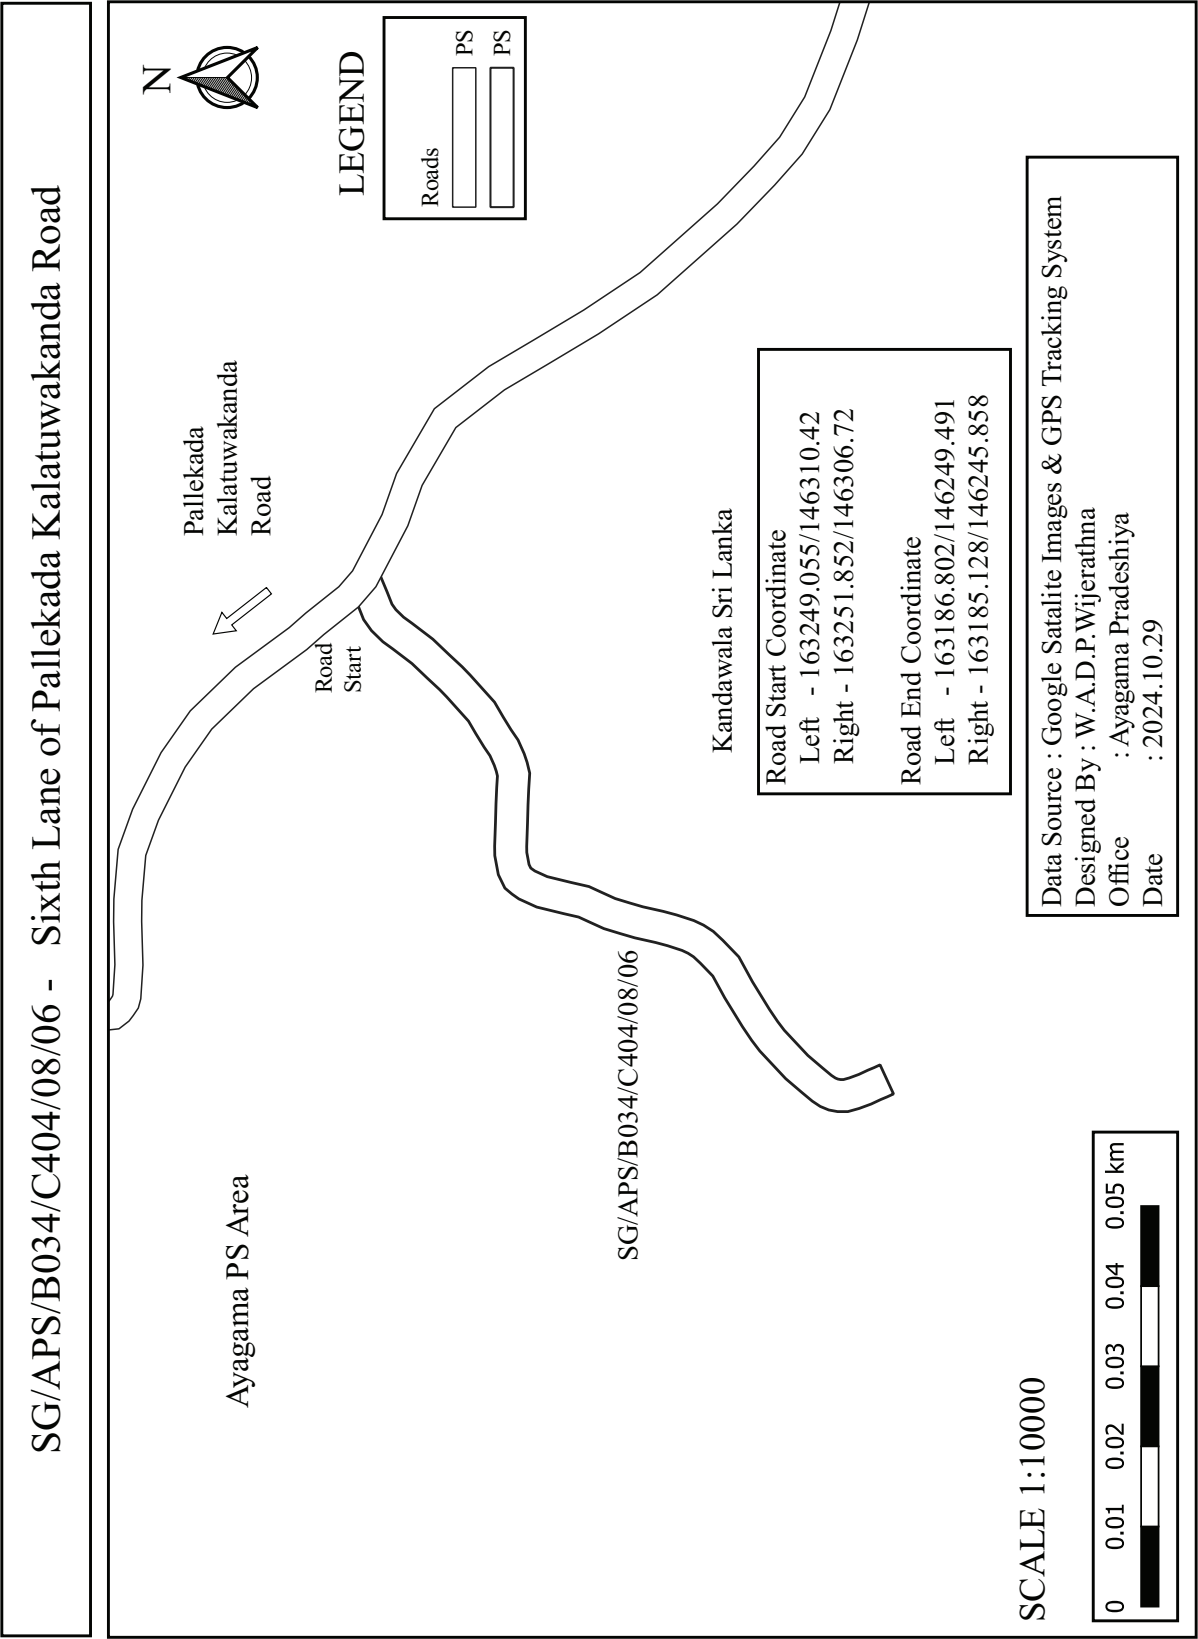


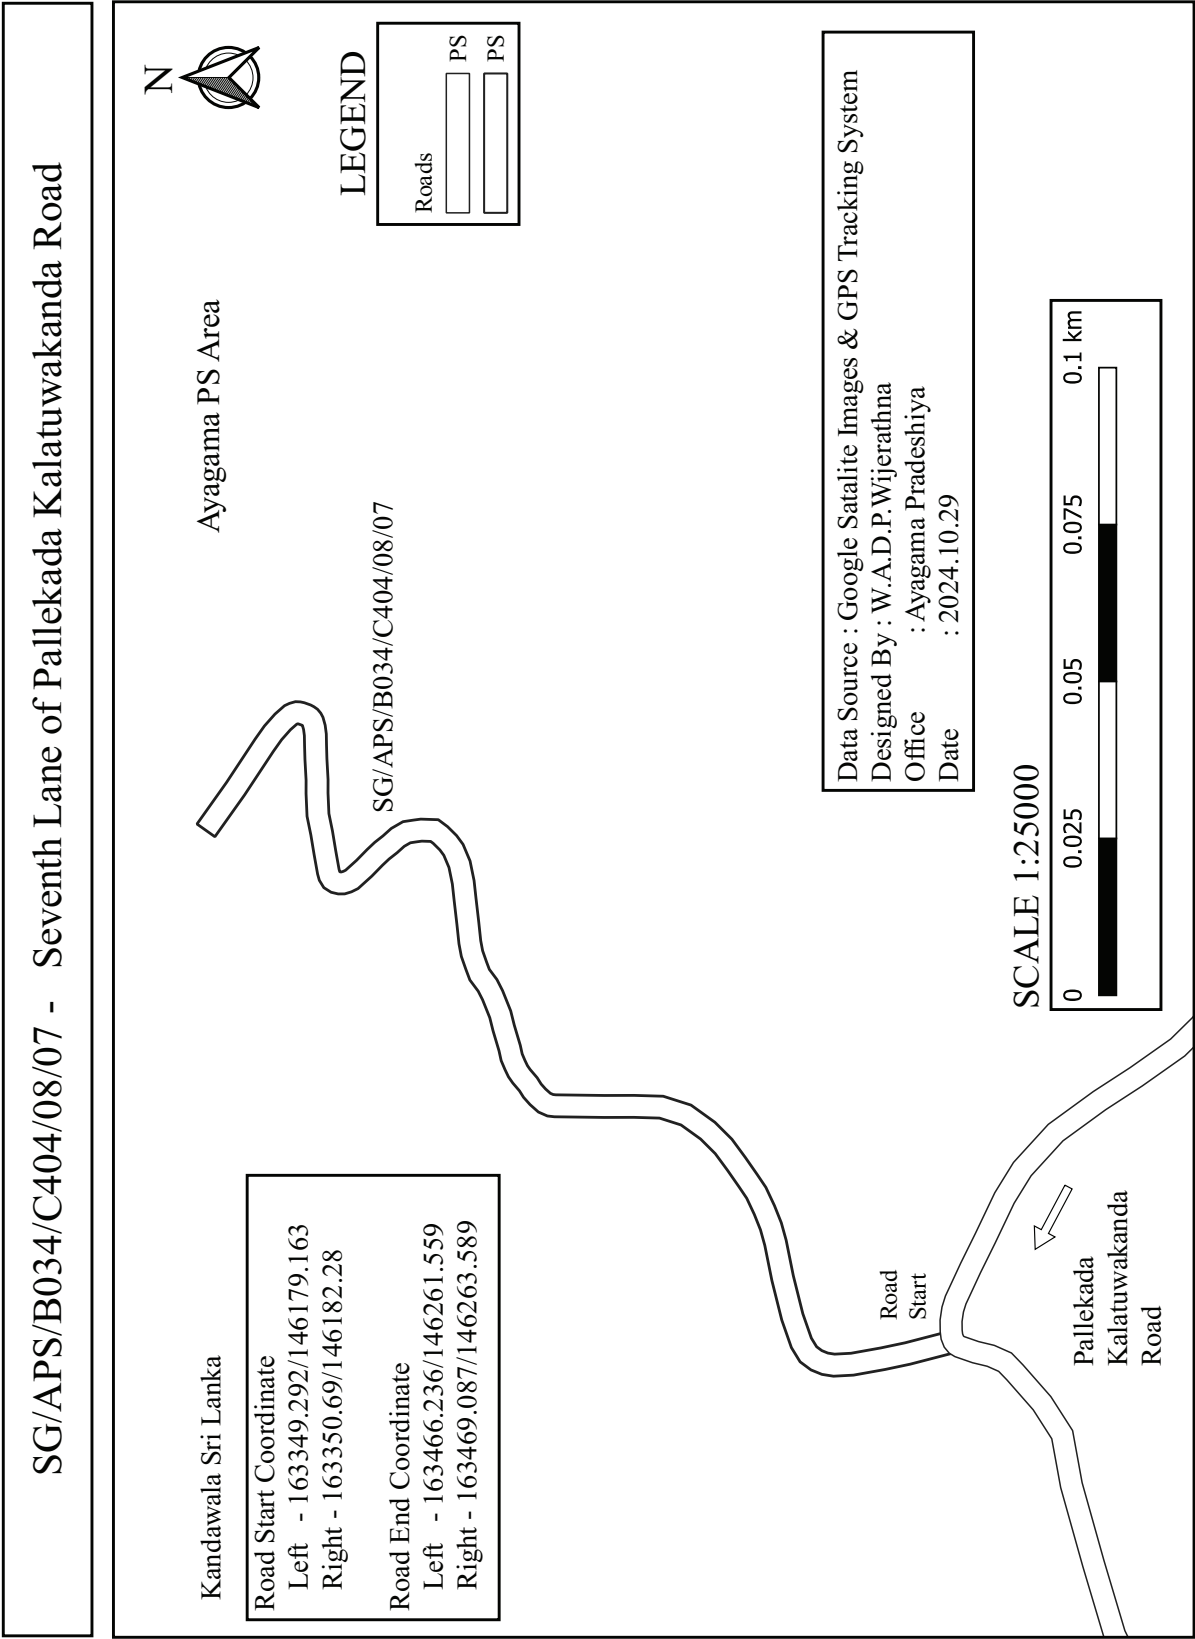


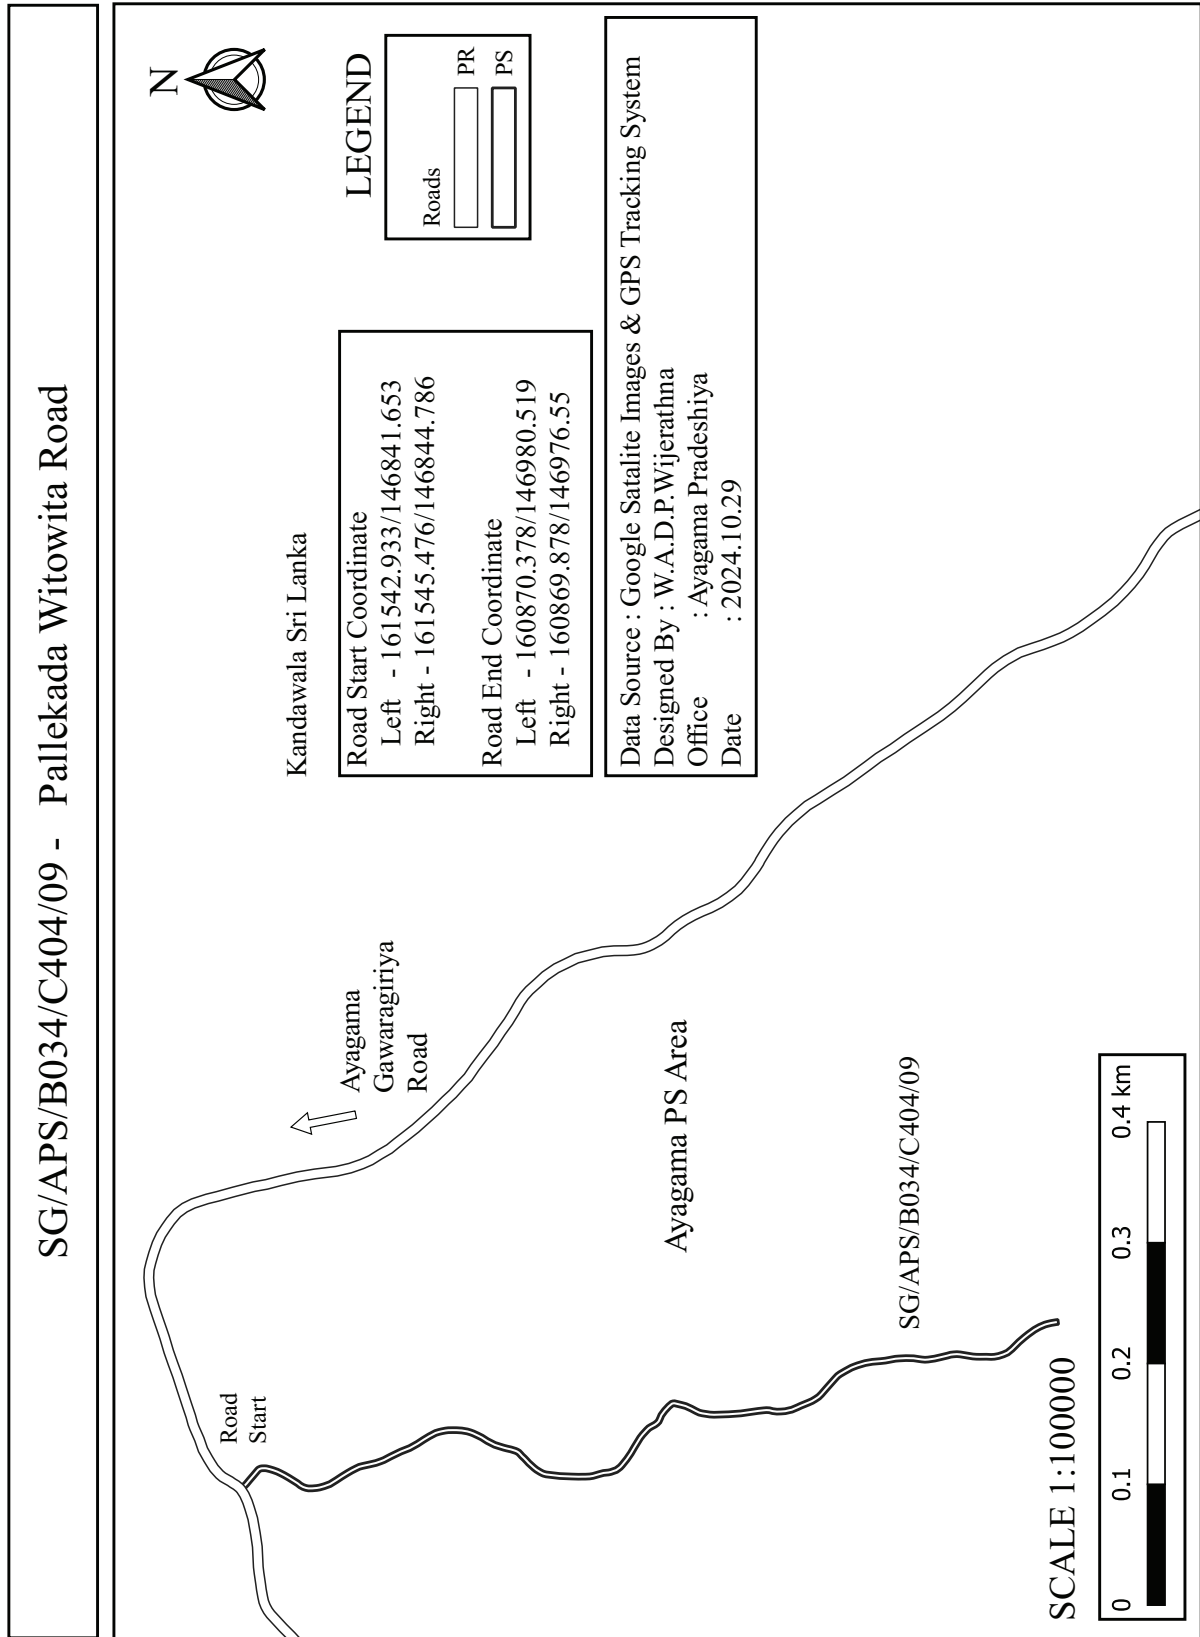


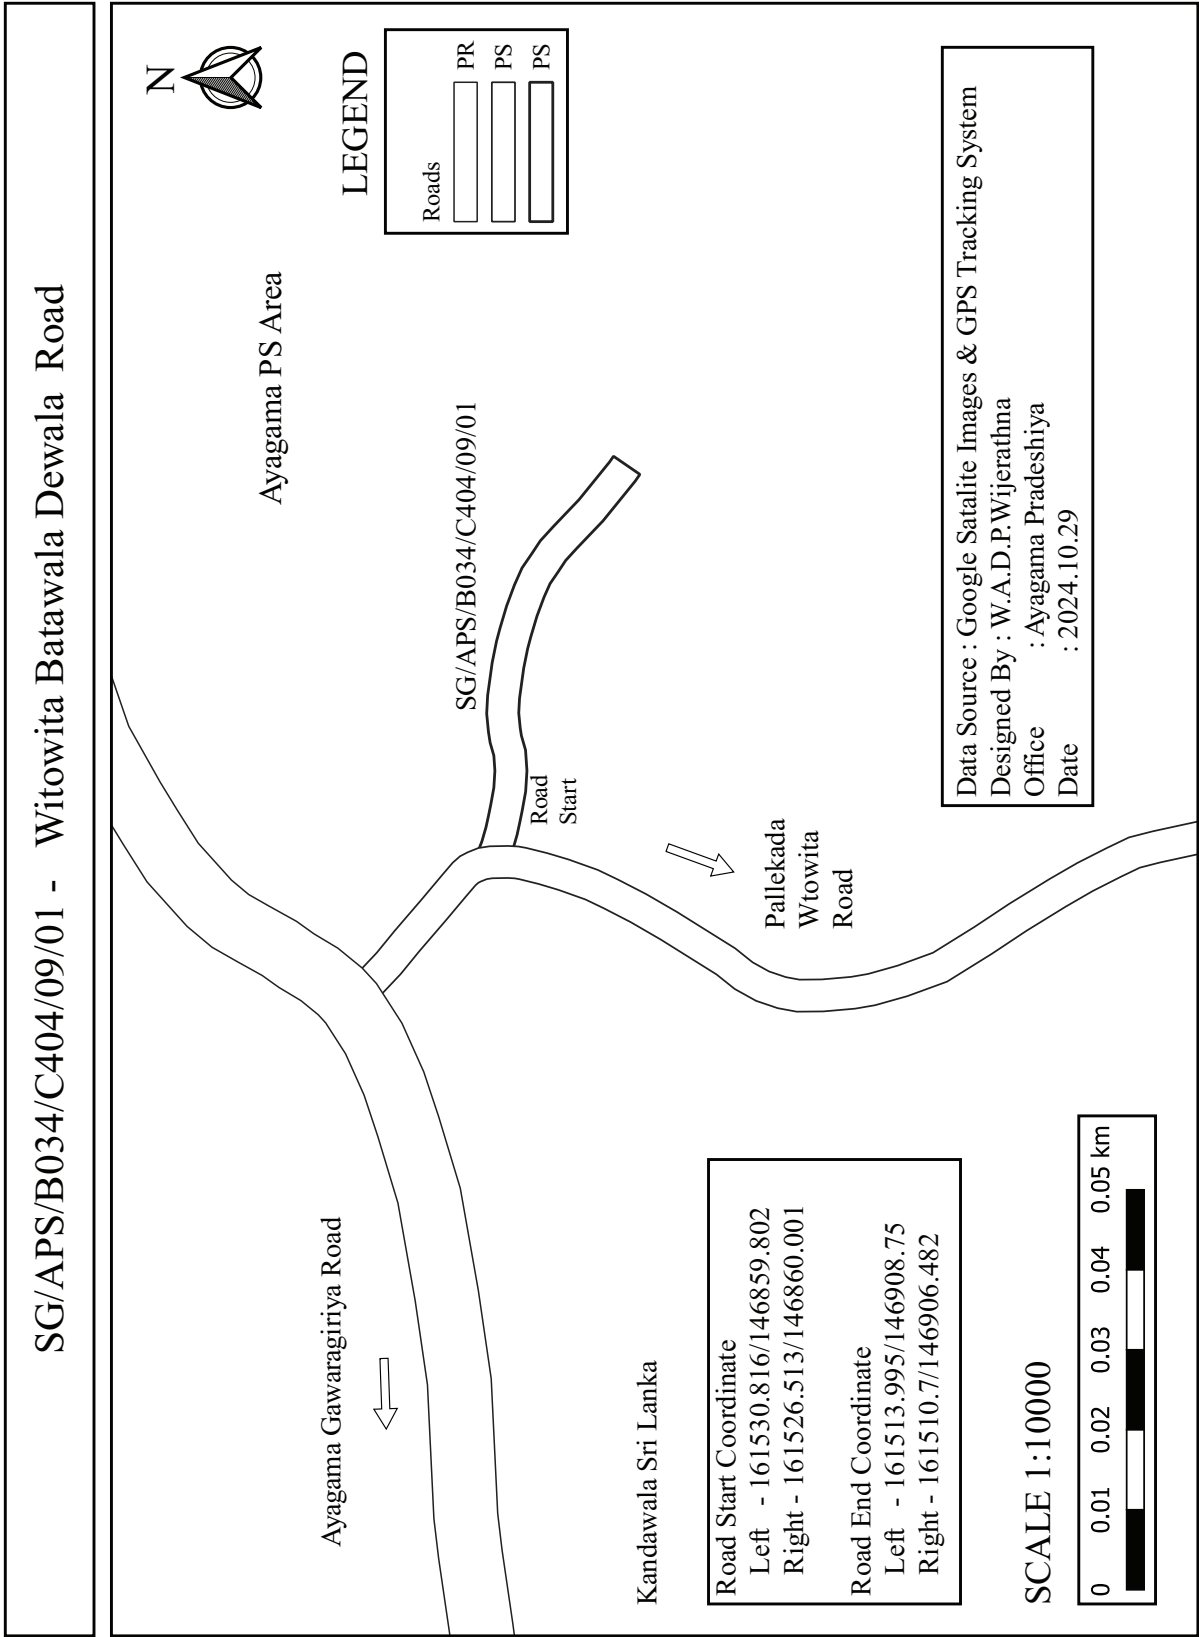


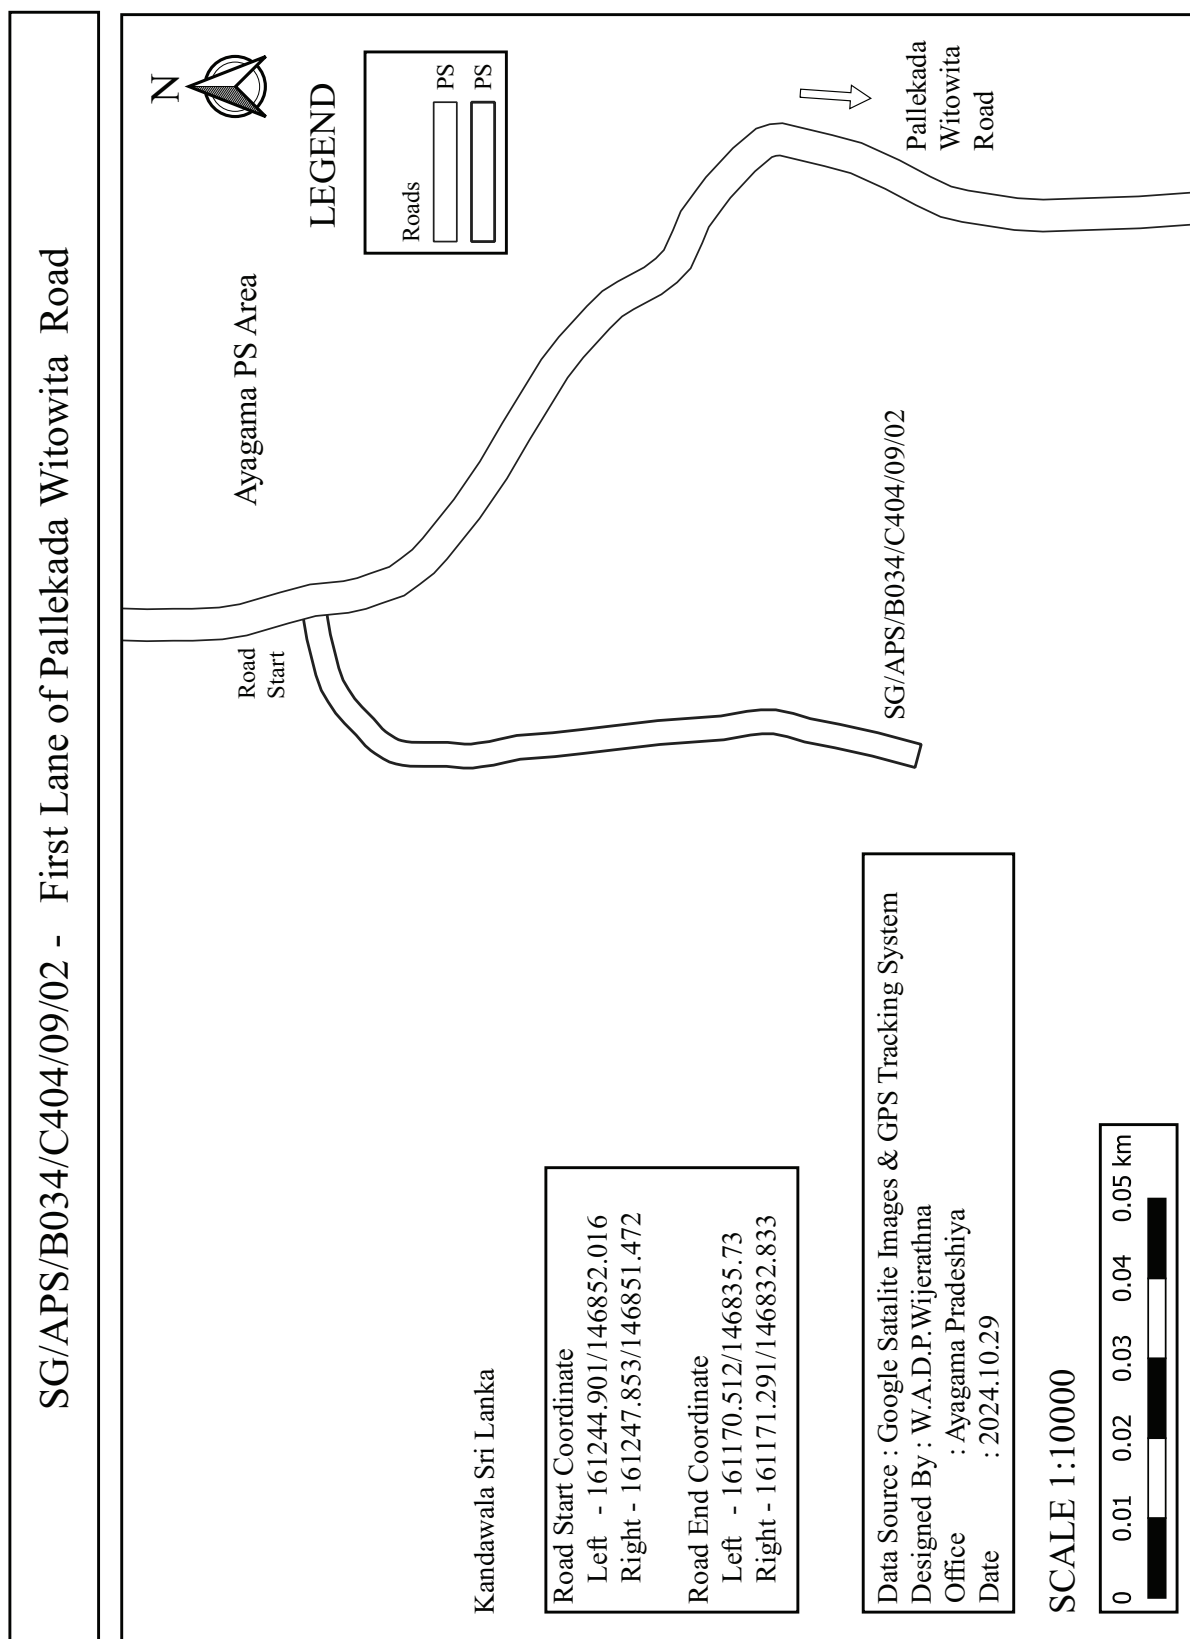

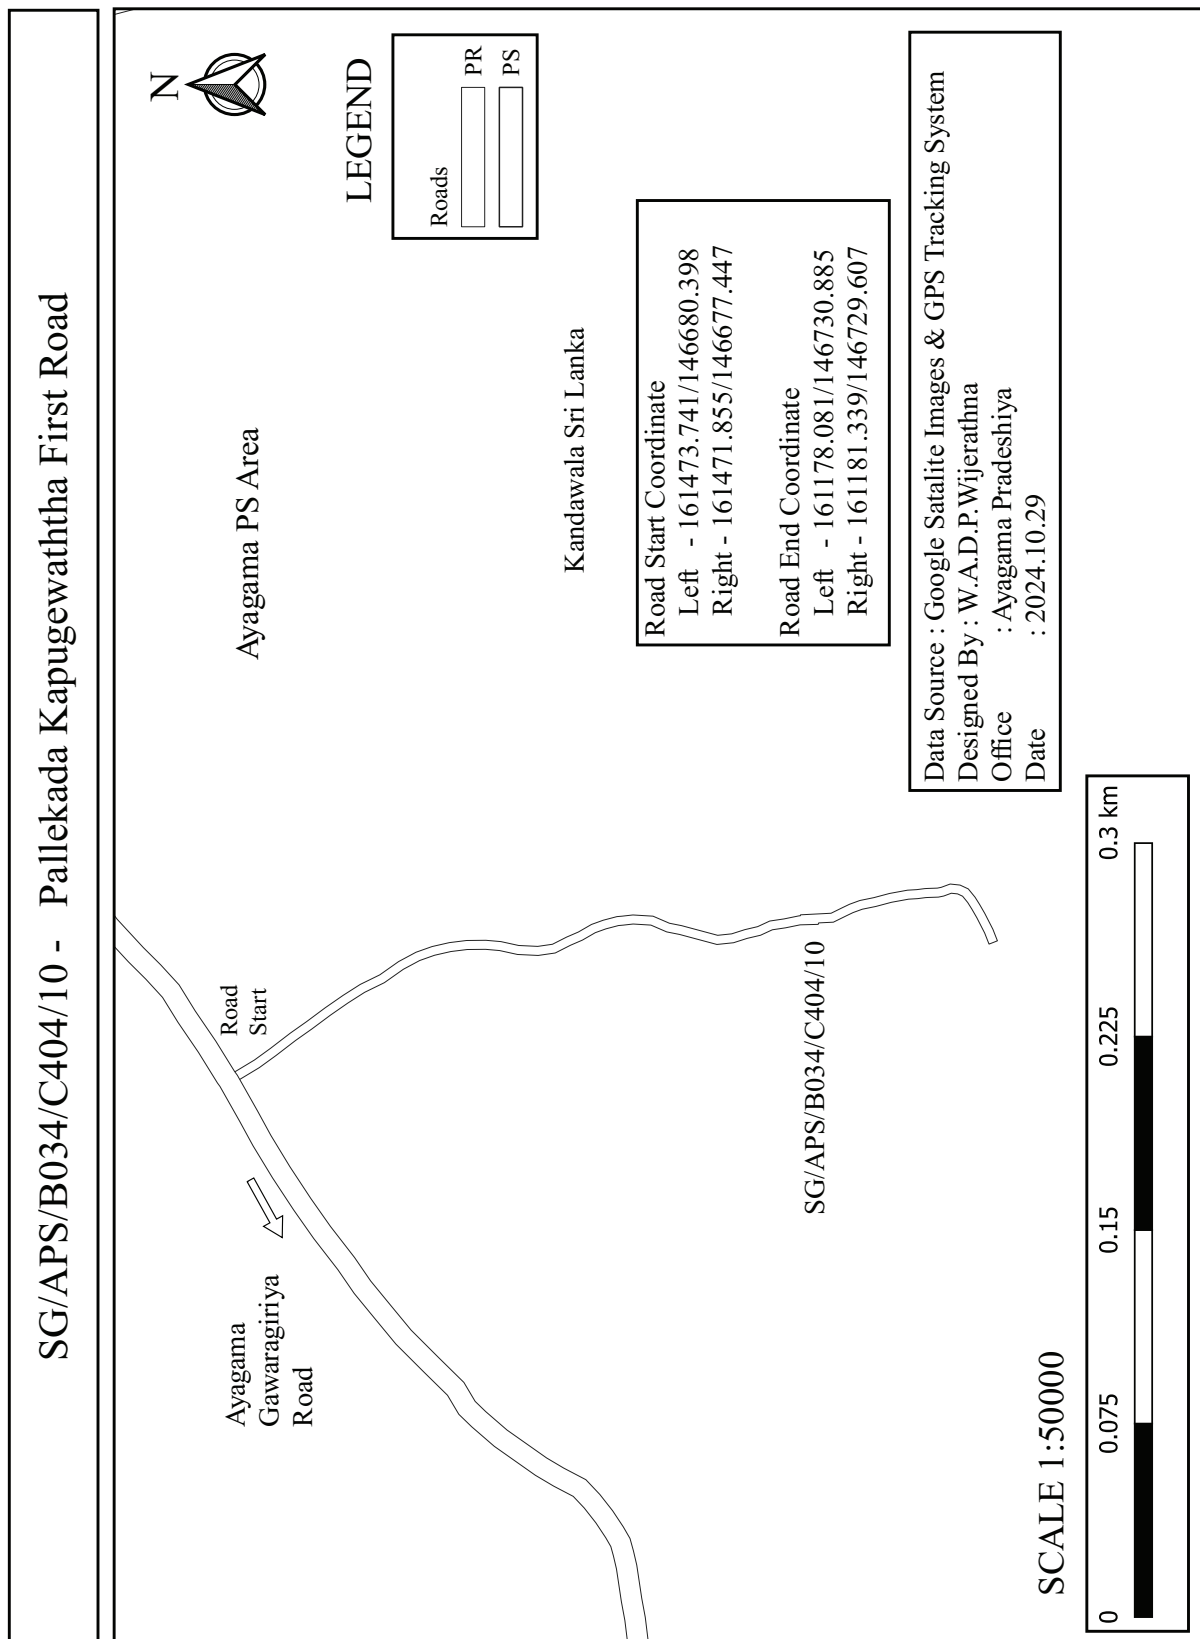

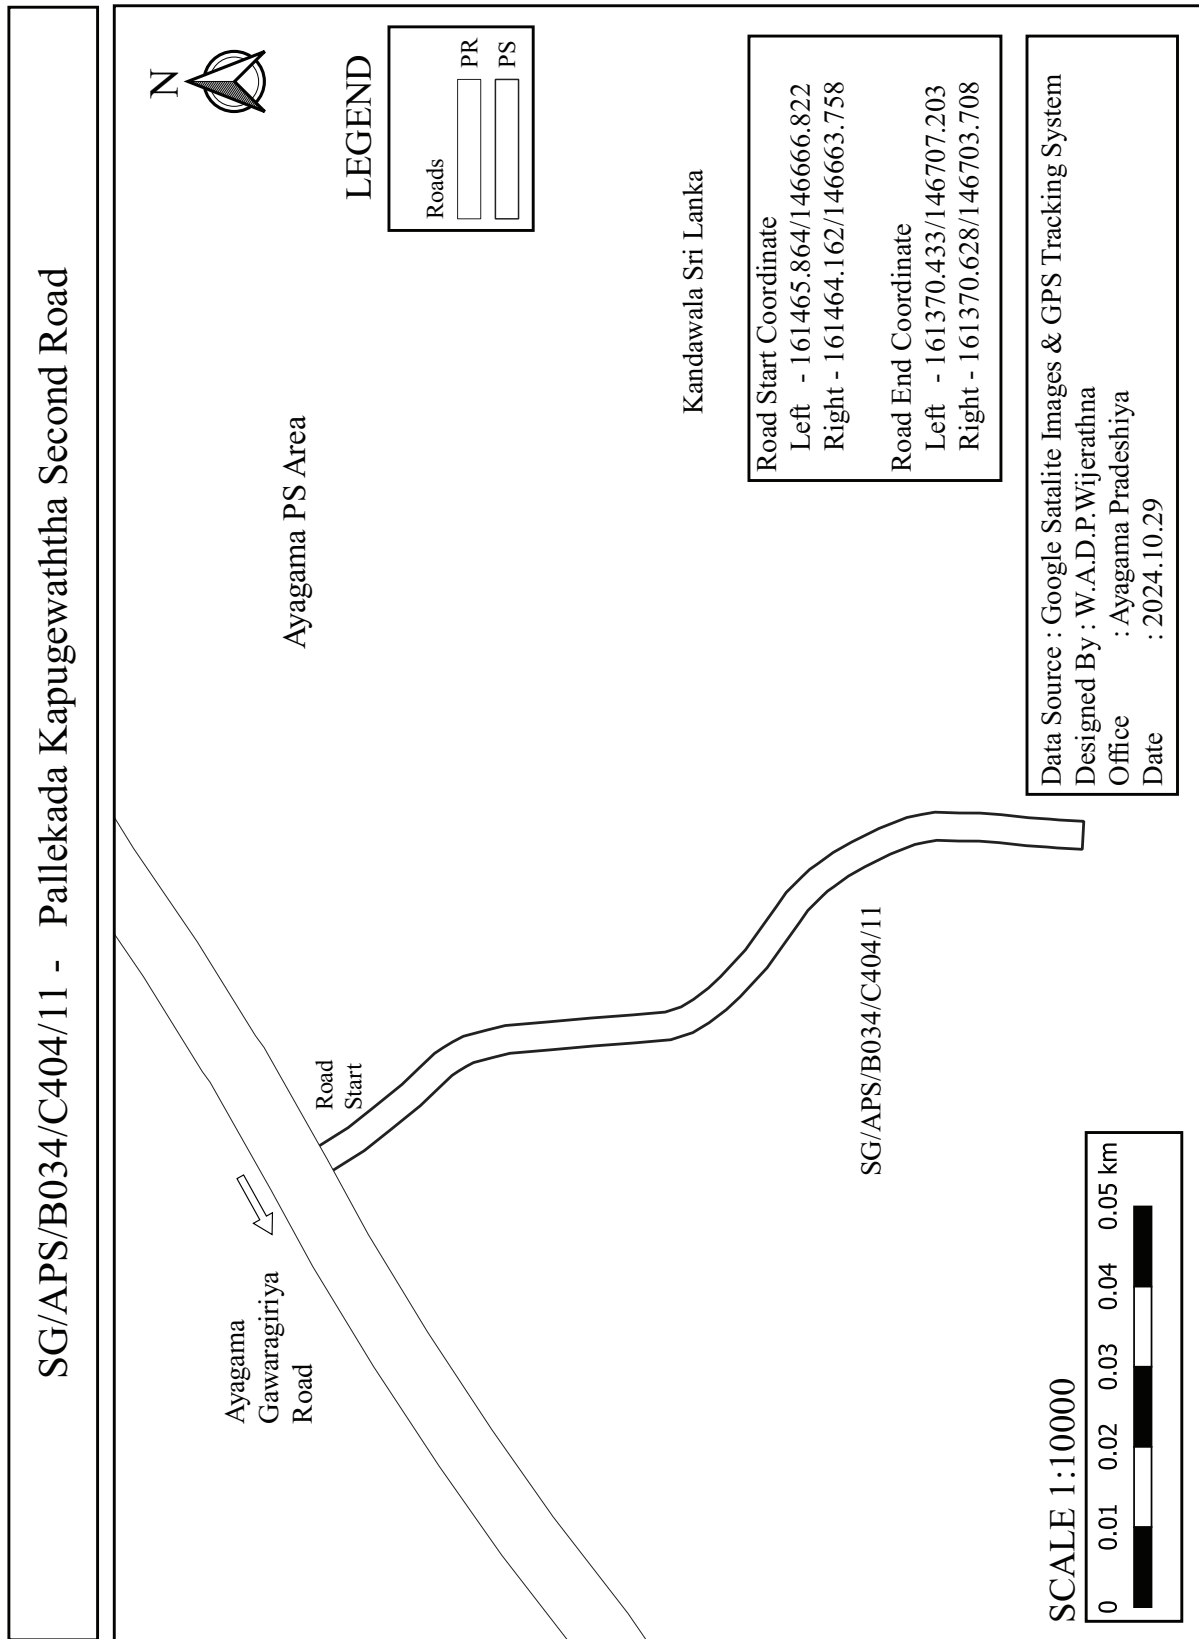

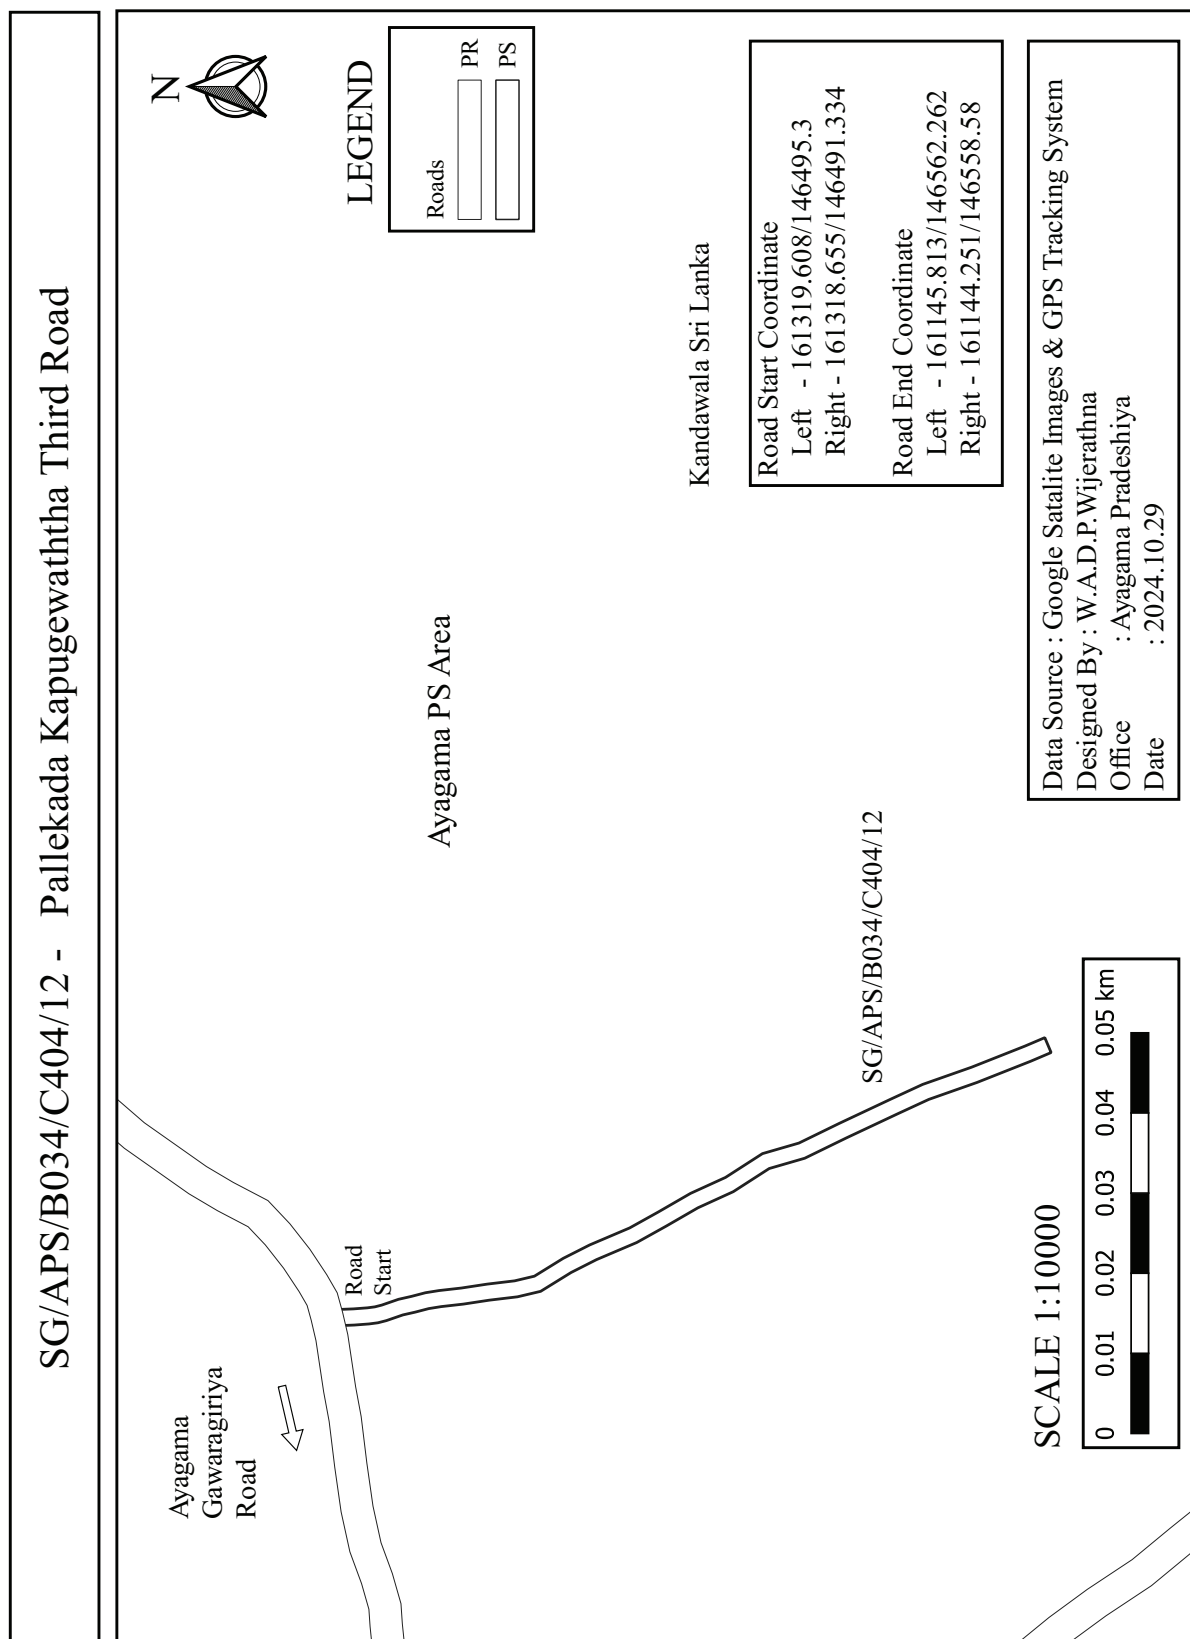

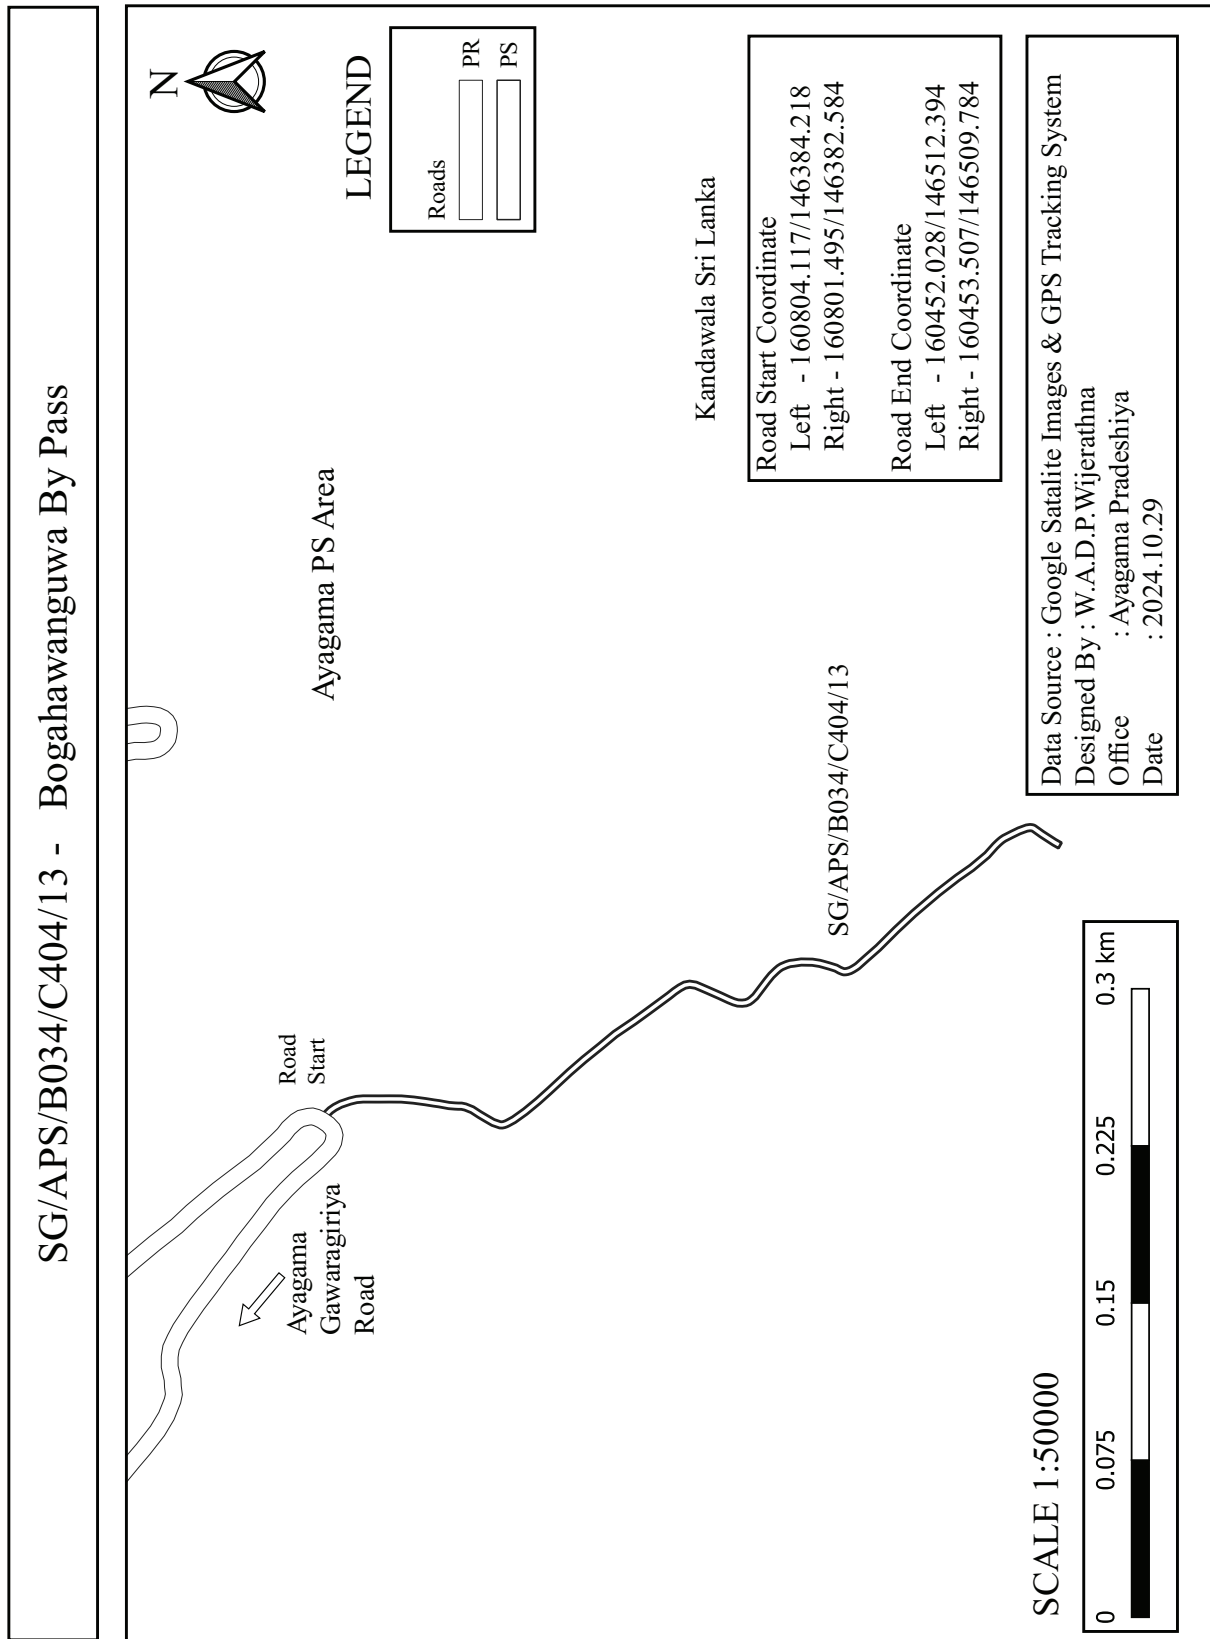

SCALE 1:50000

0 0.075 0.15 0.225 0.3 km


SG/APS/B034/C404/13


Data Source : Google Satalite Images & GPS Tracking System


Designed By : W.A.D.P.Wijerathna


Office : Ayagama Pradeshiya


Date : 2024.10.29

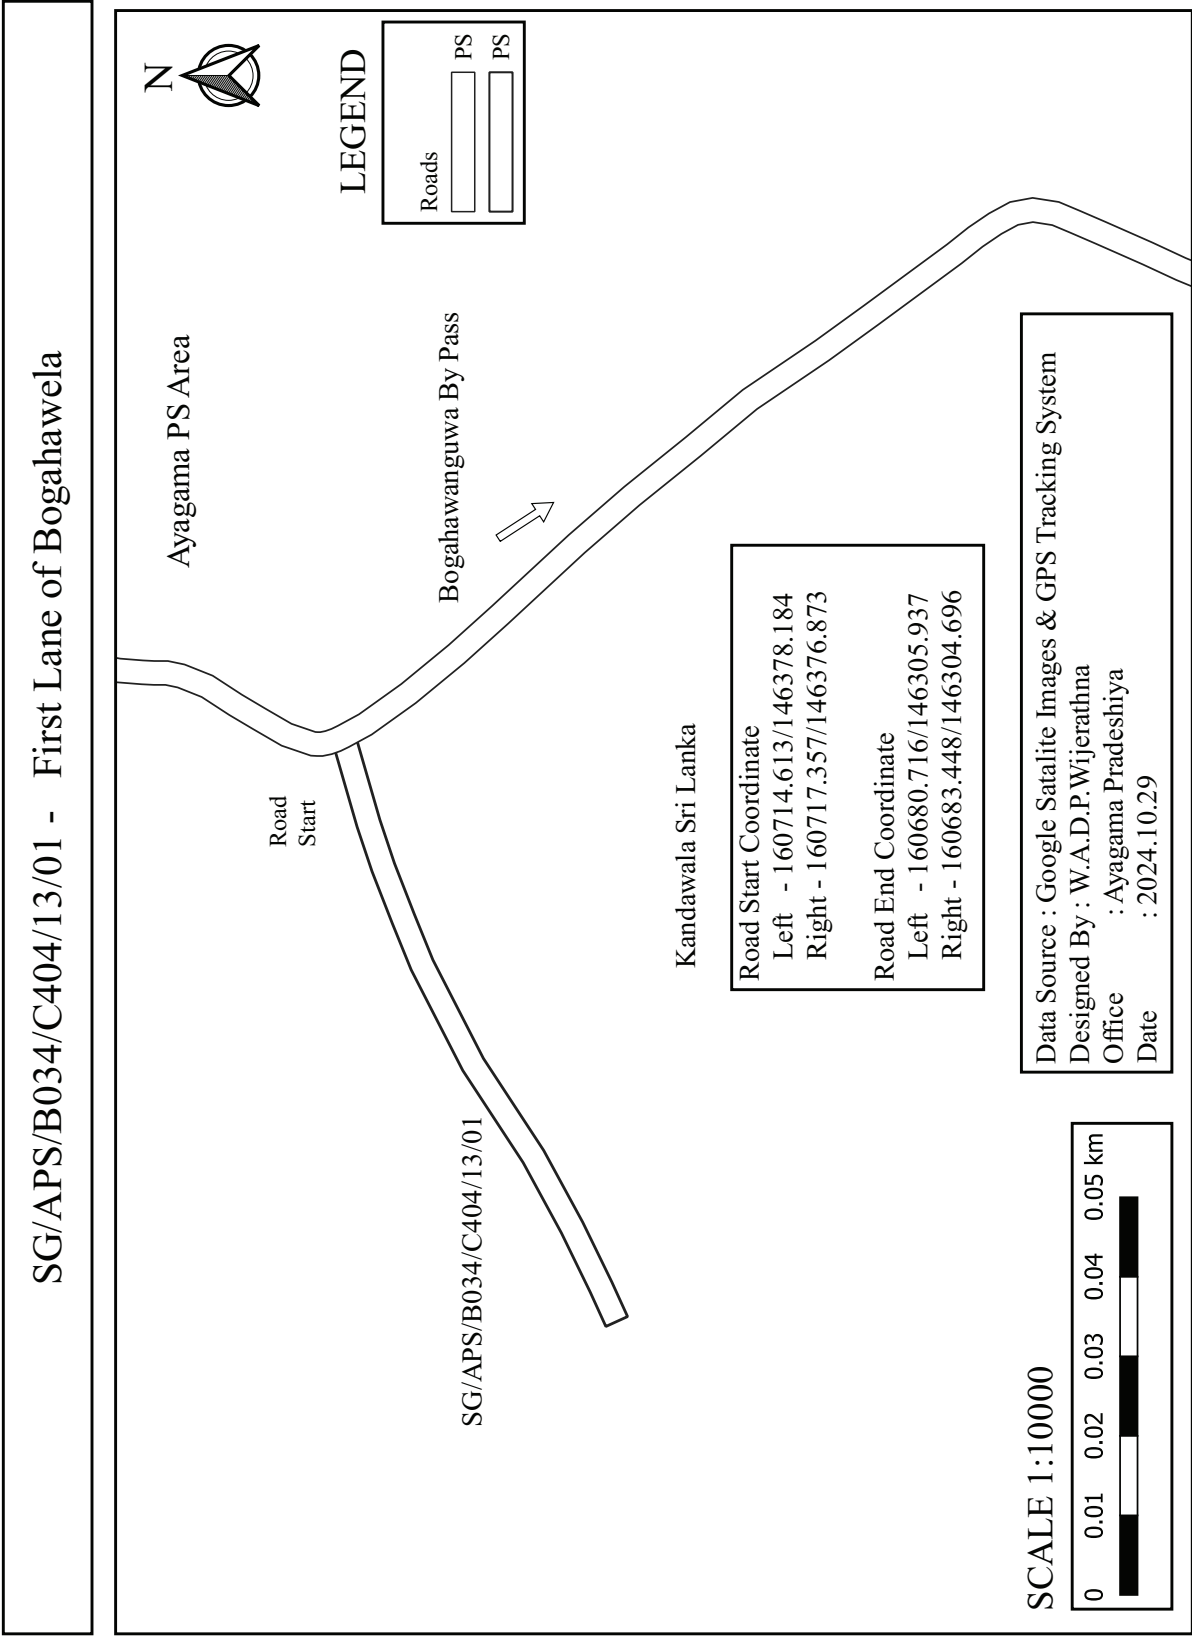

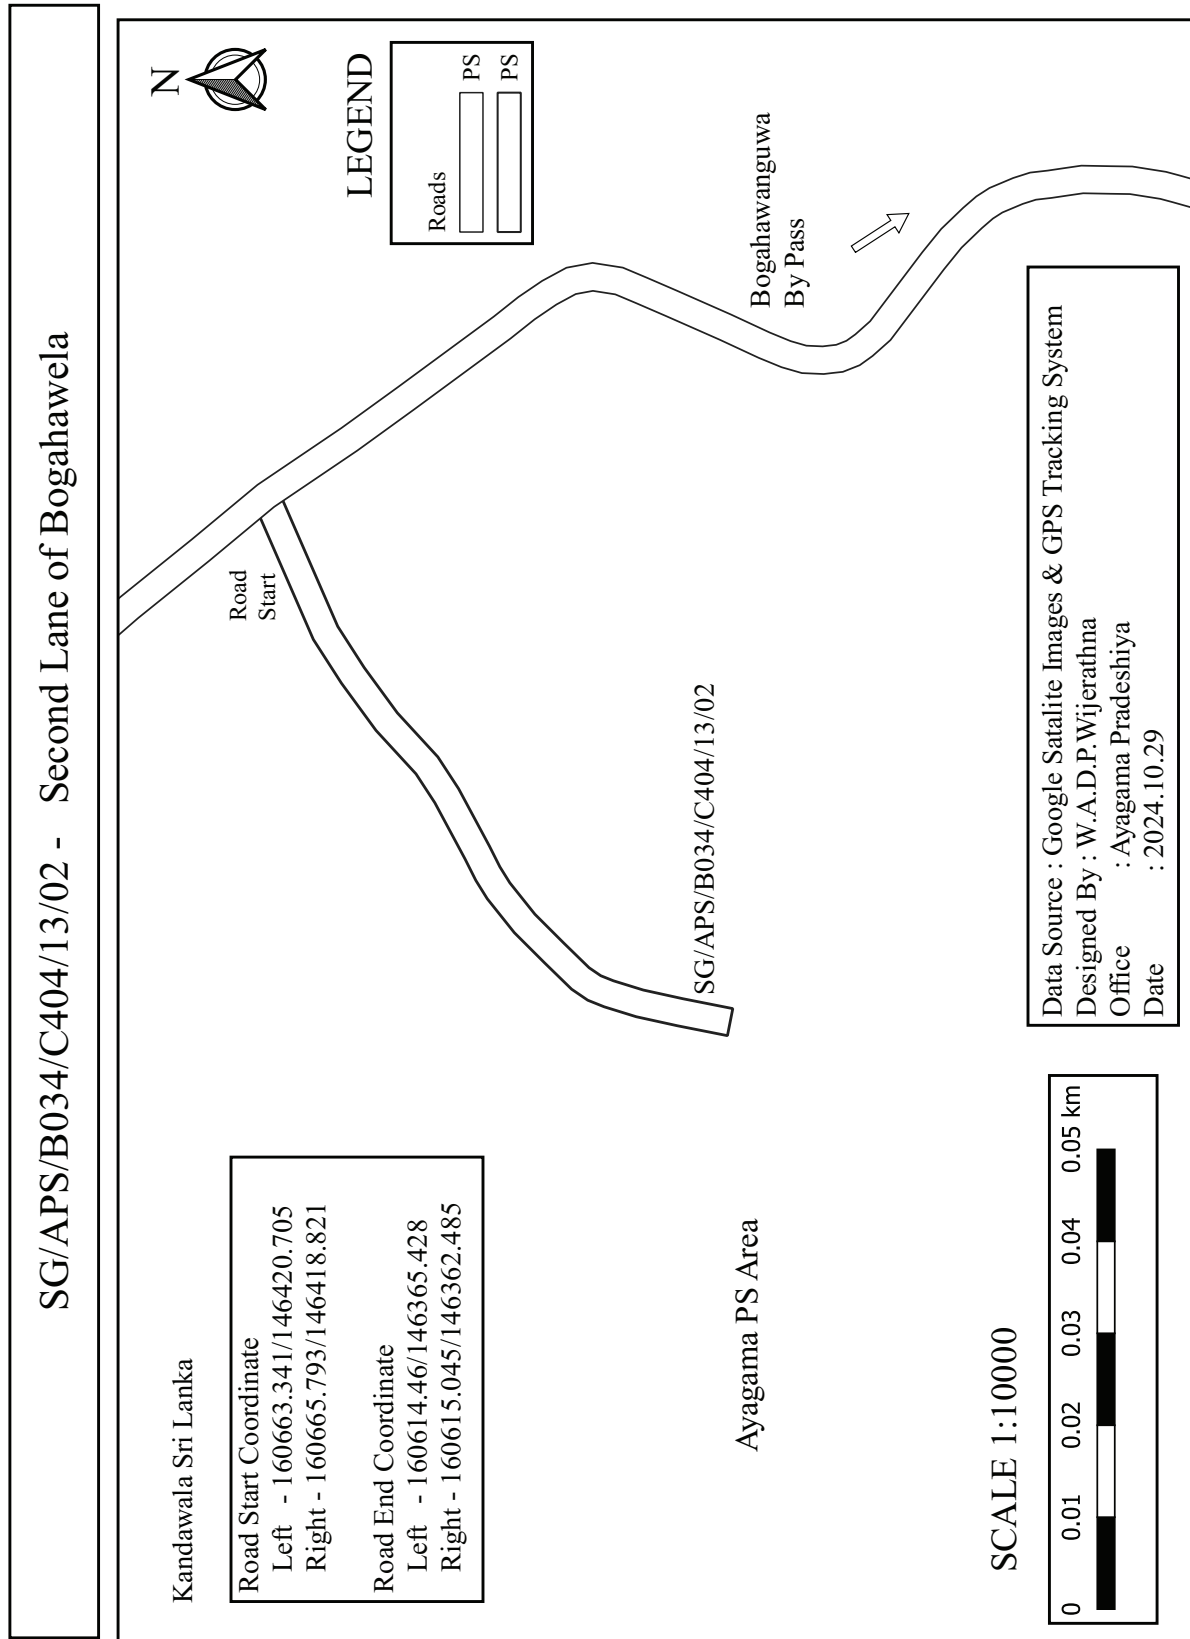


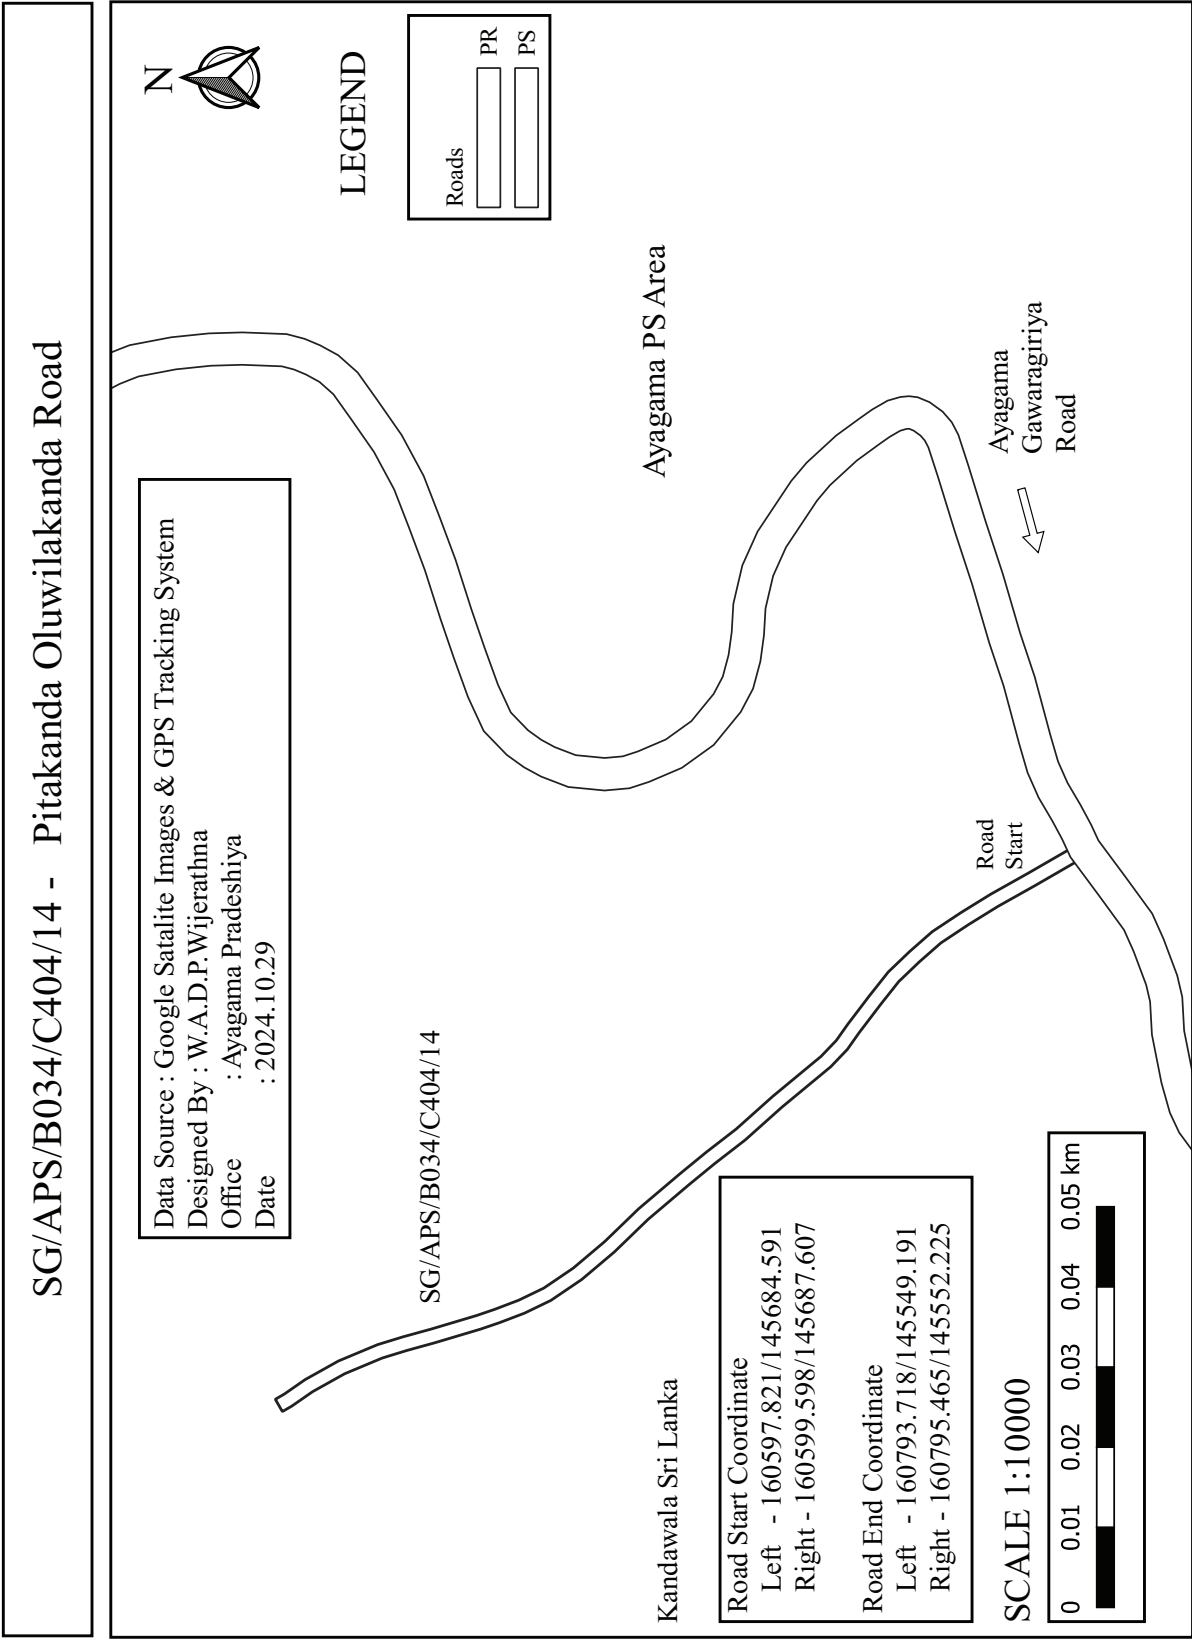


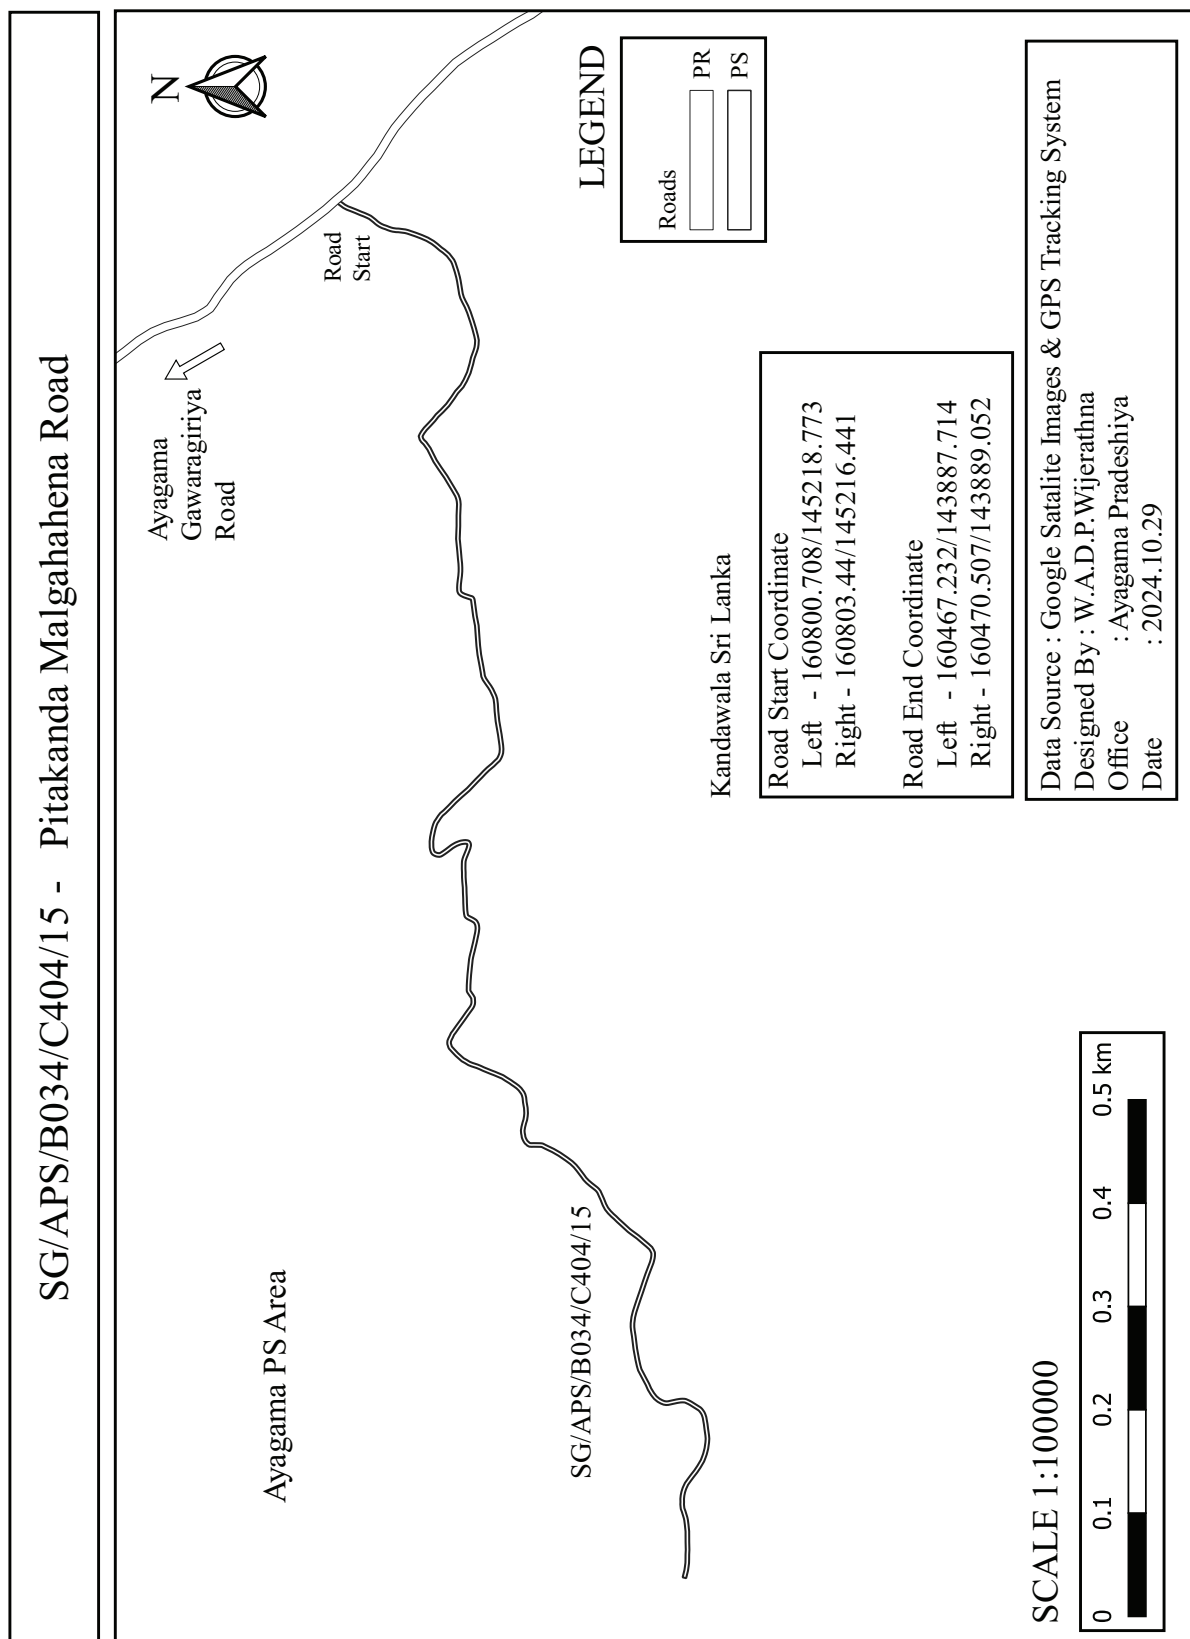


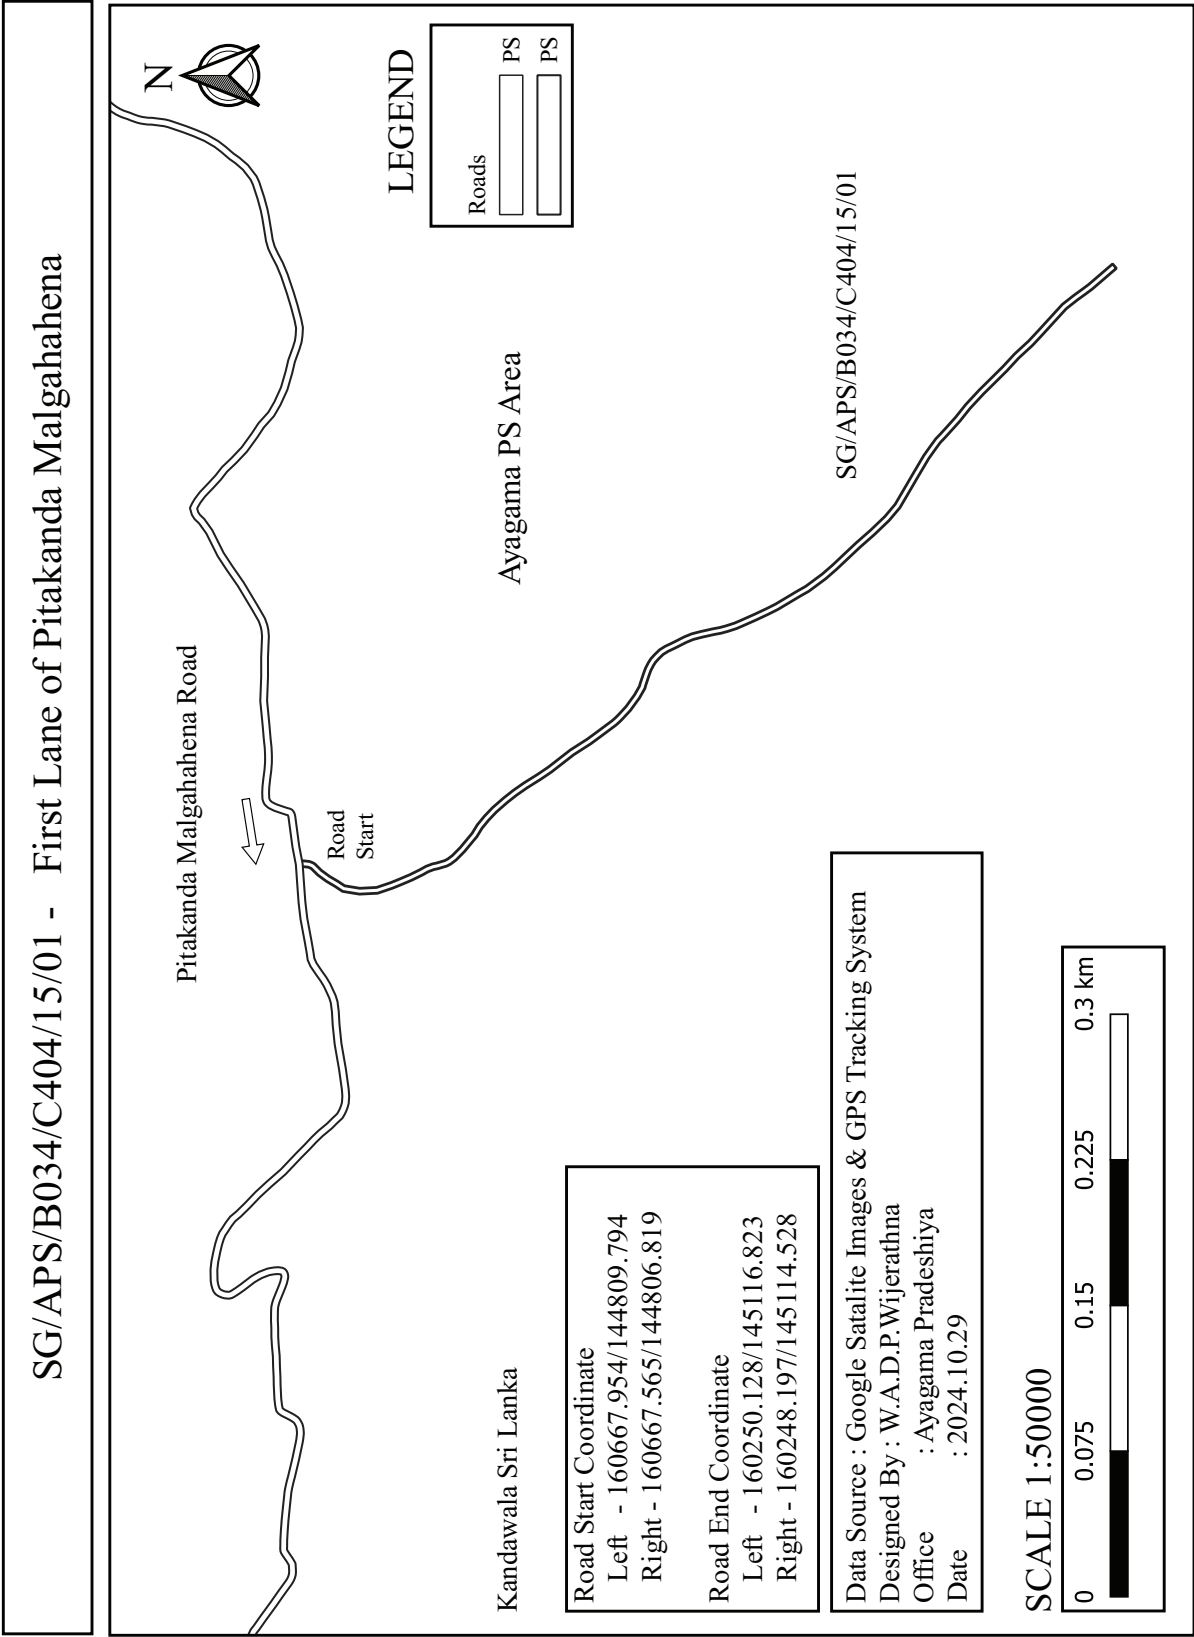



SG/APS/B034/C404/16 - First Lane of Gawaragiriya

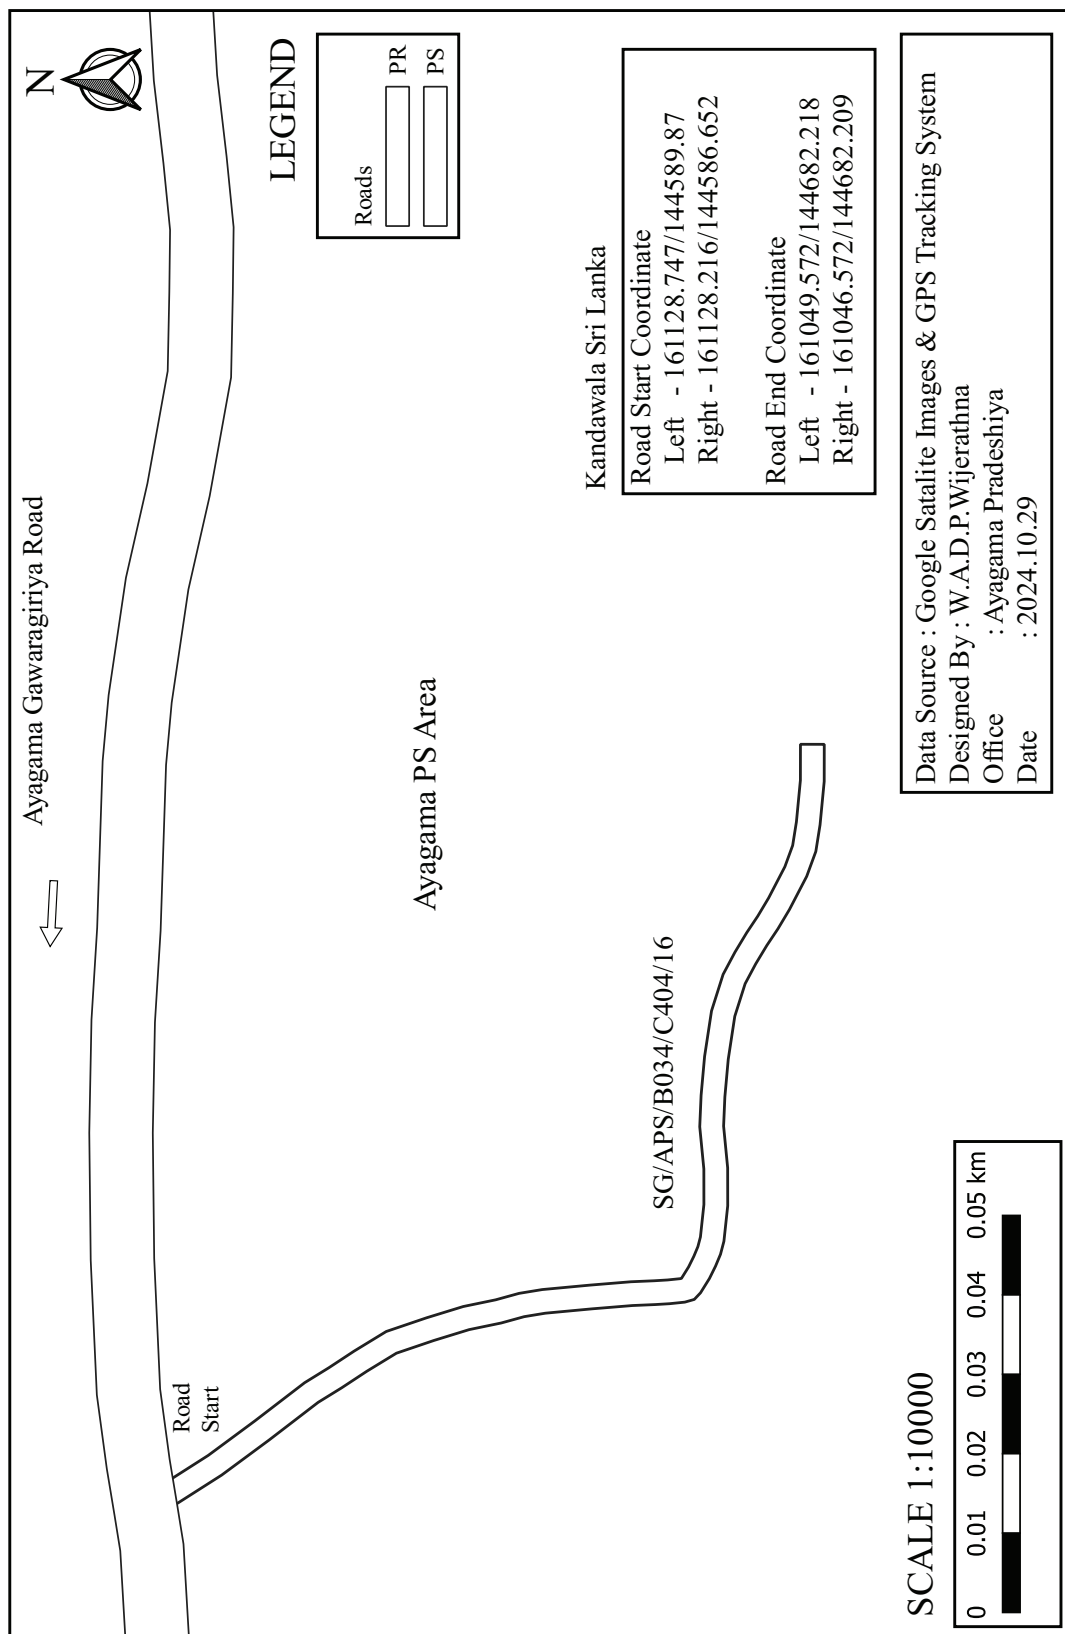


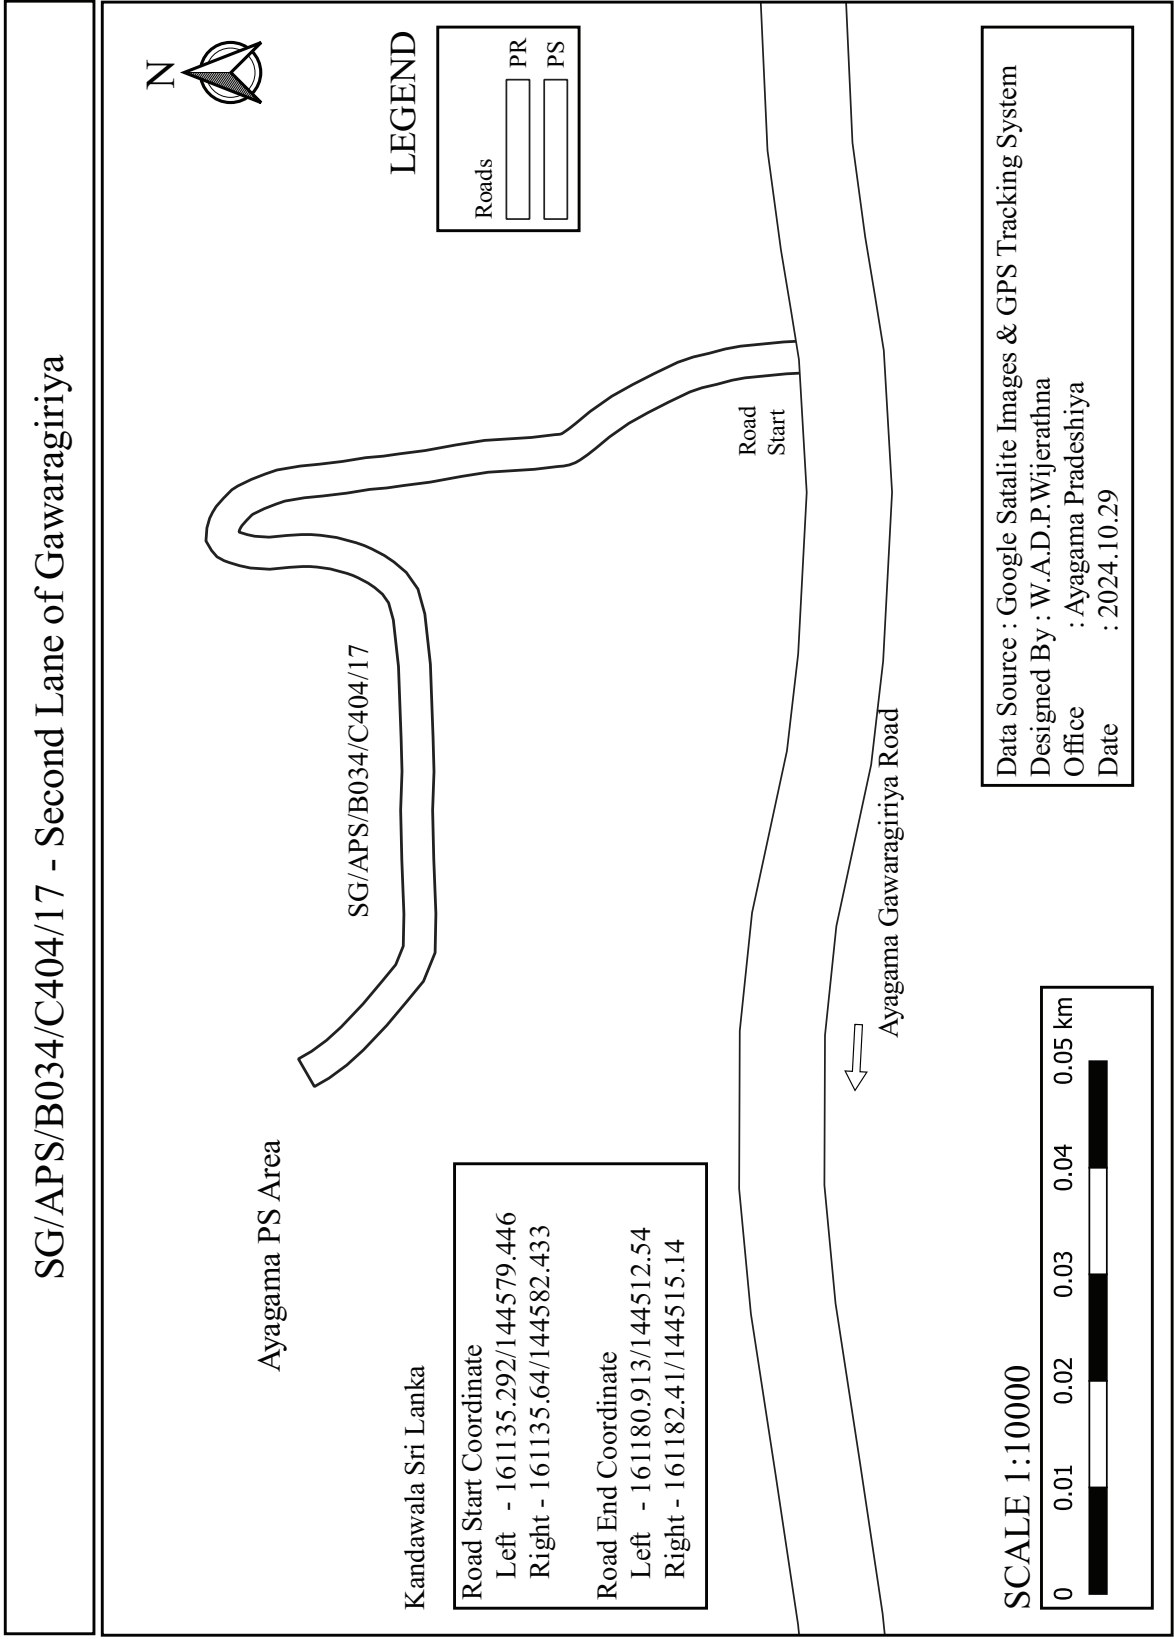

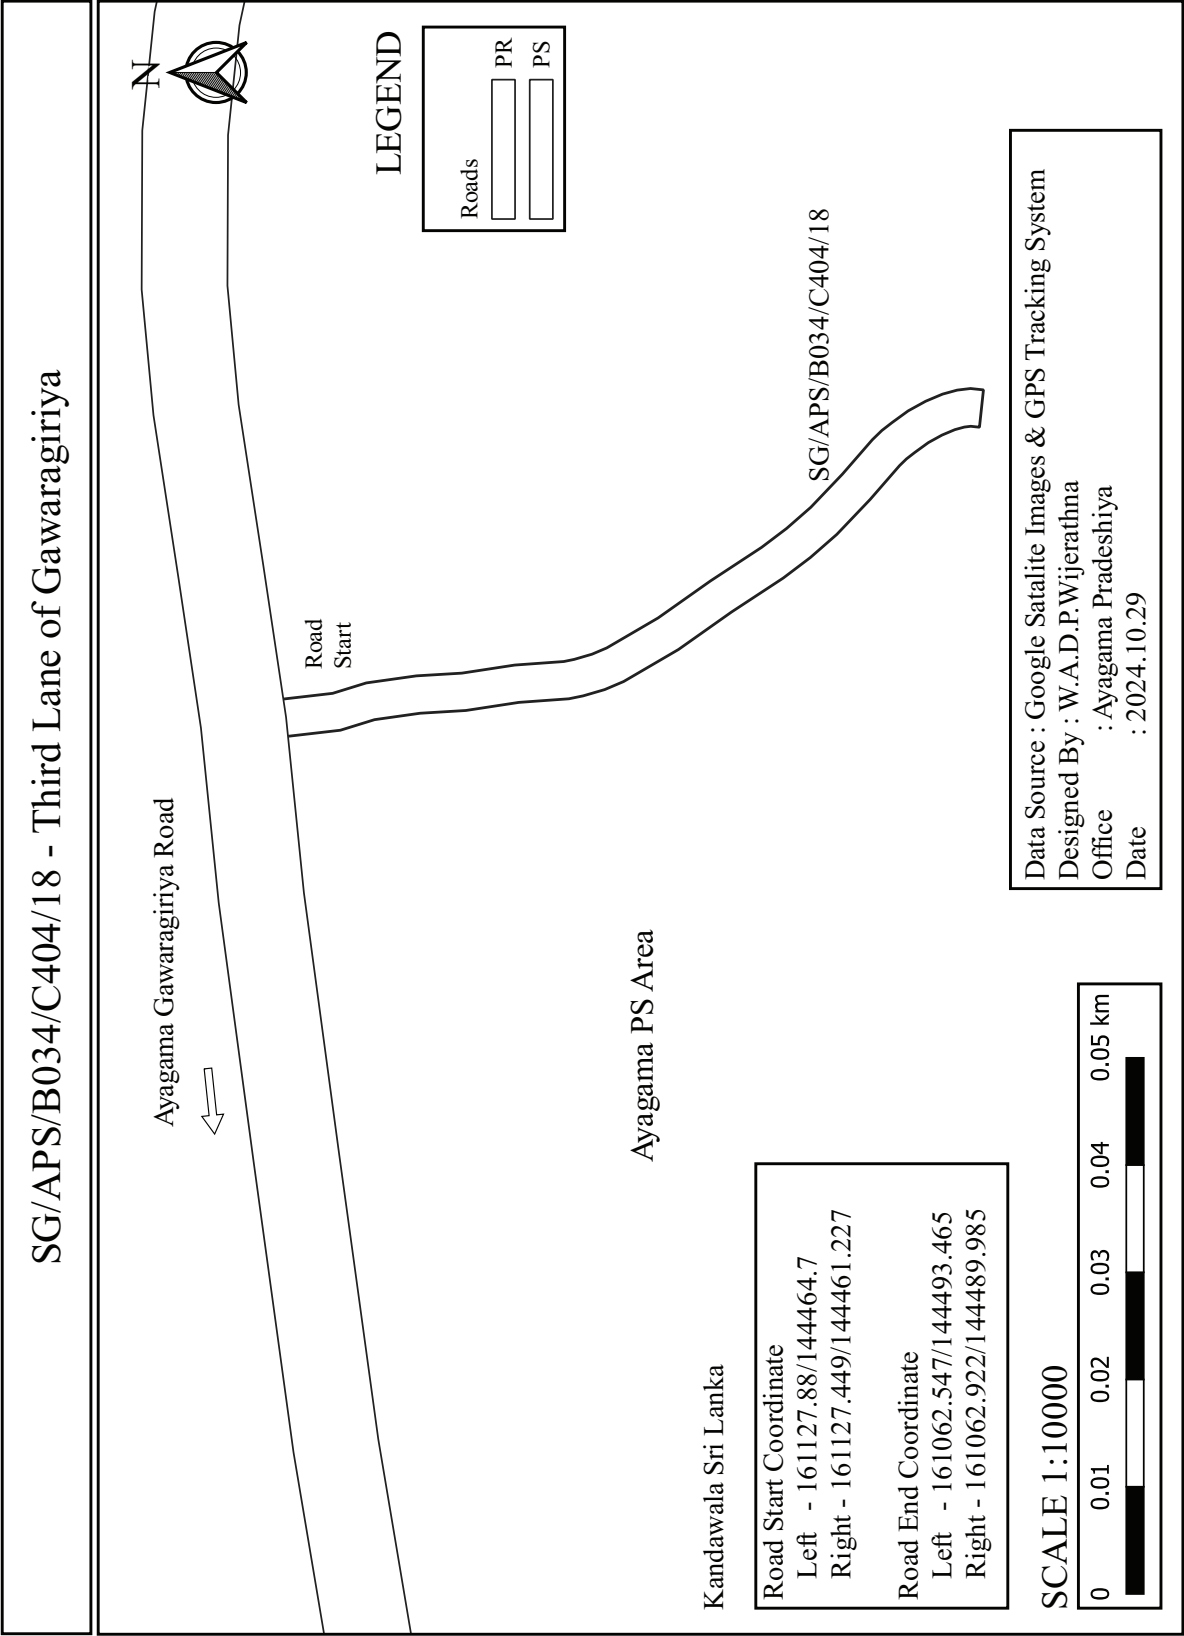


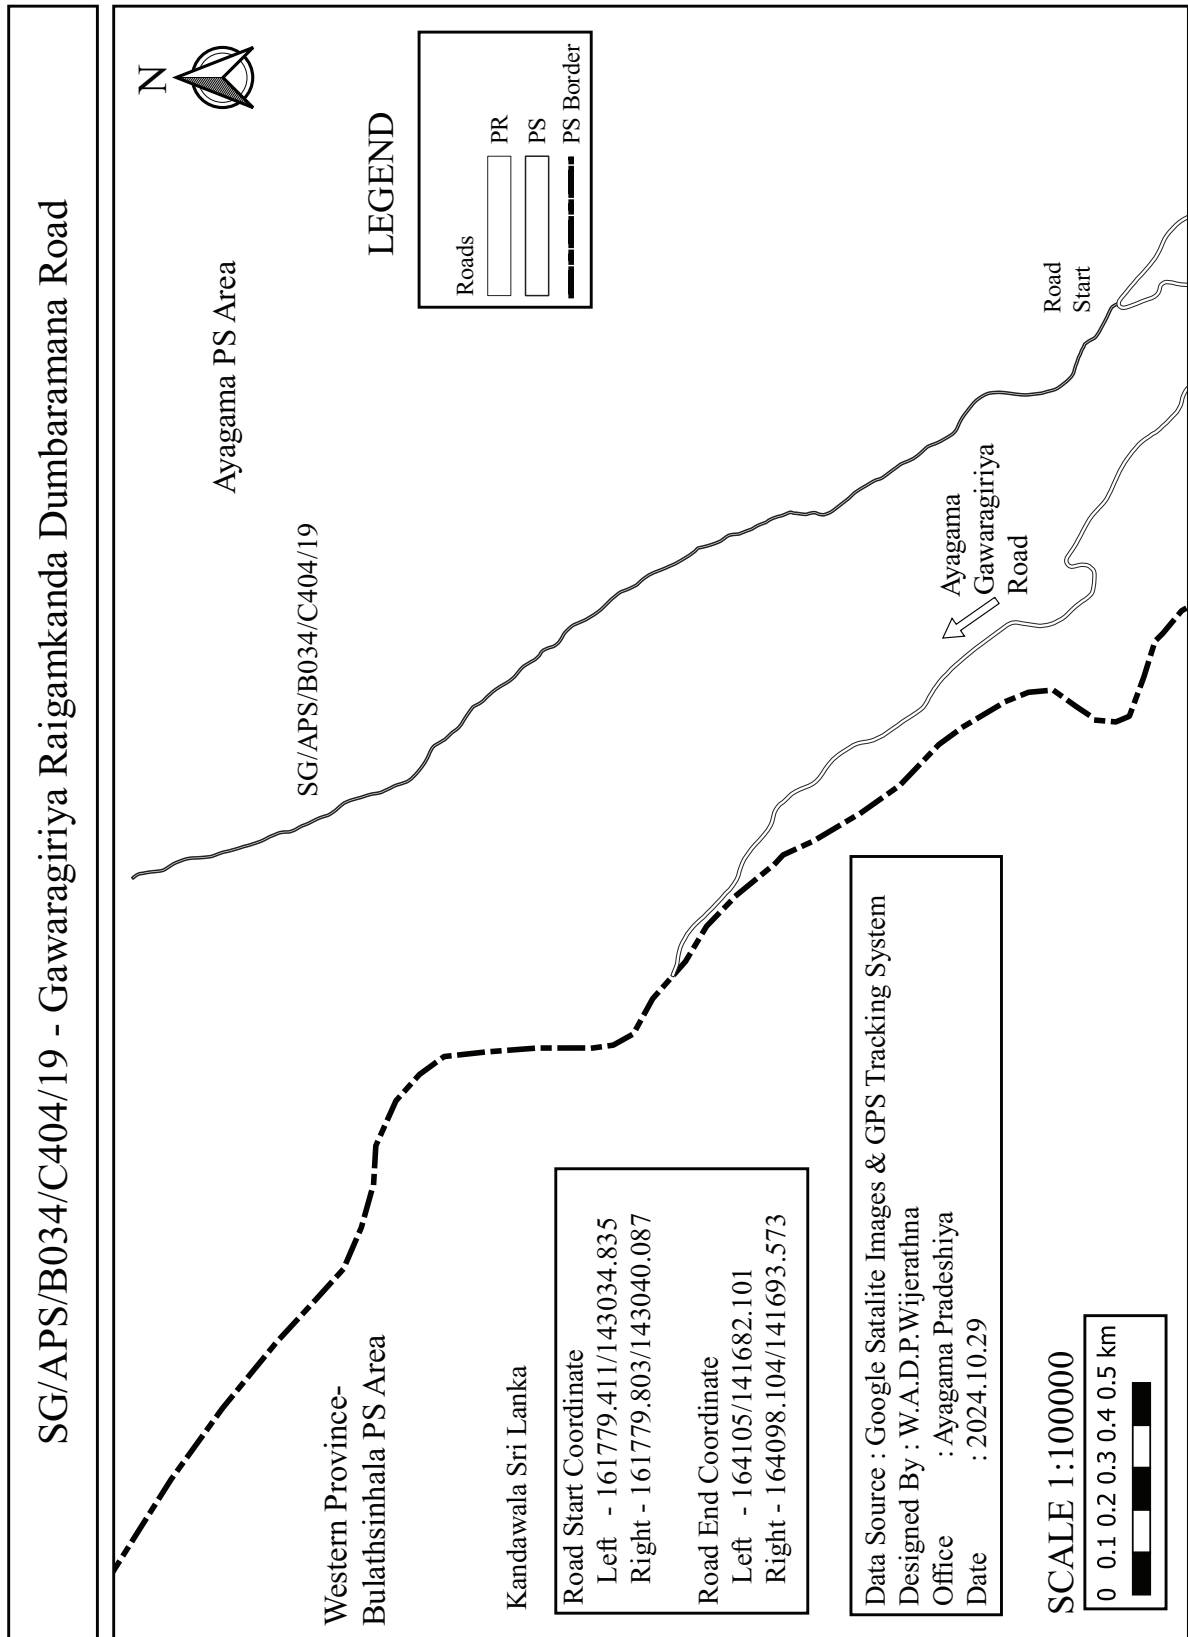


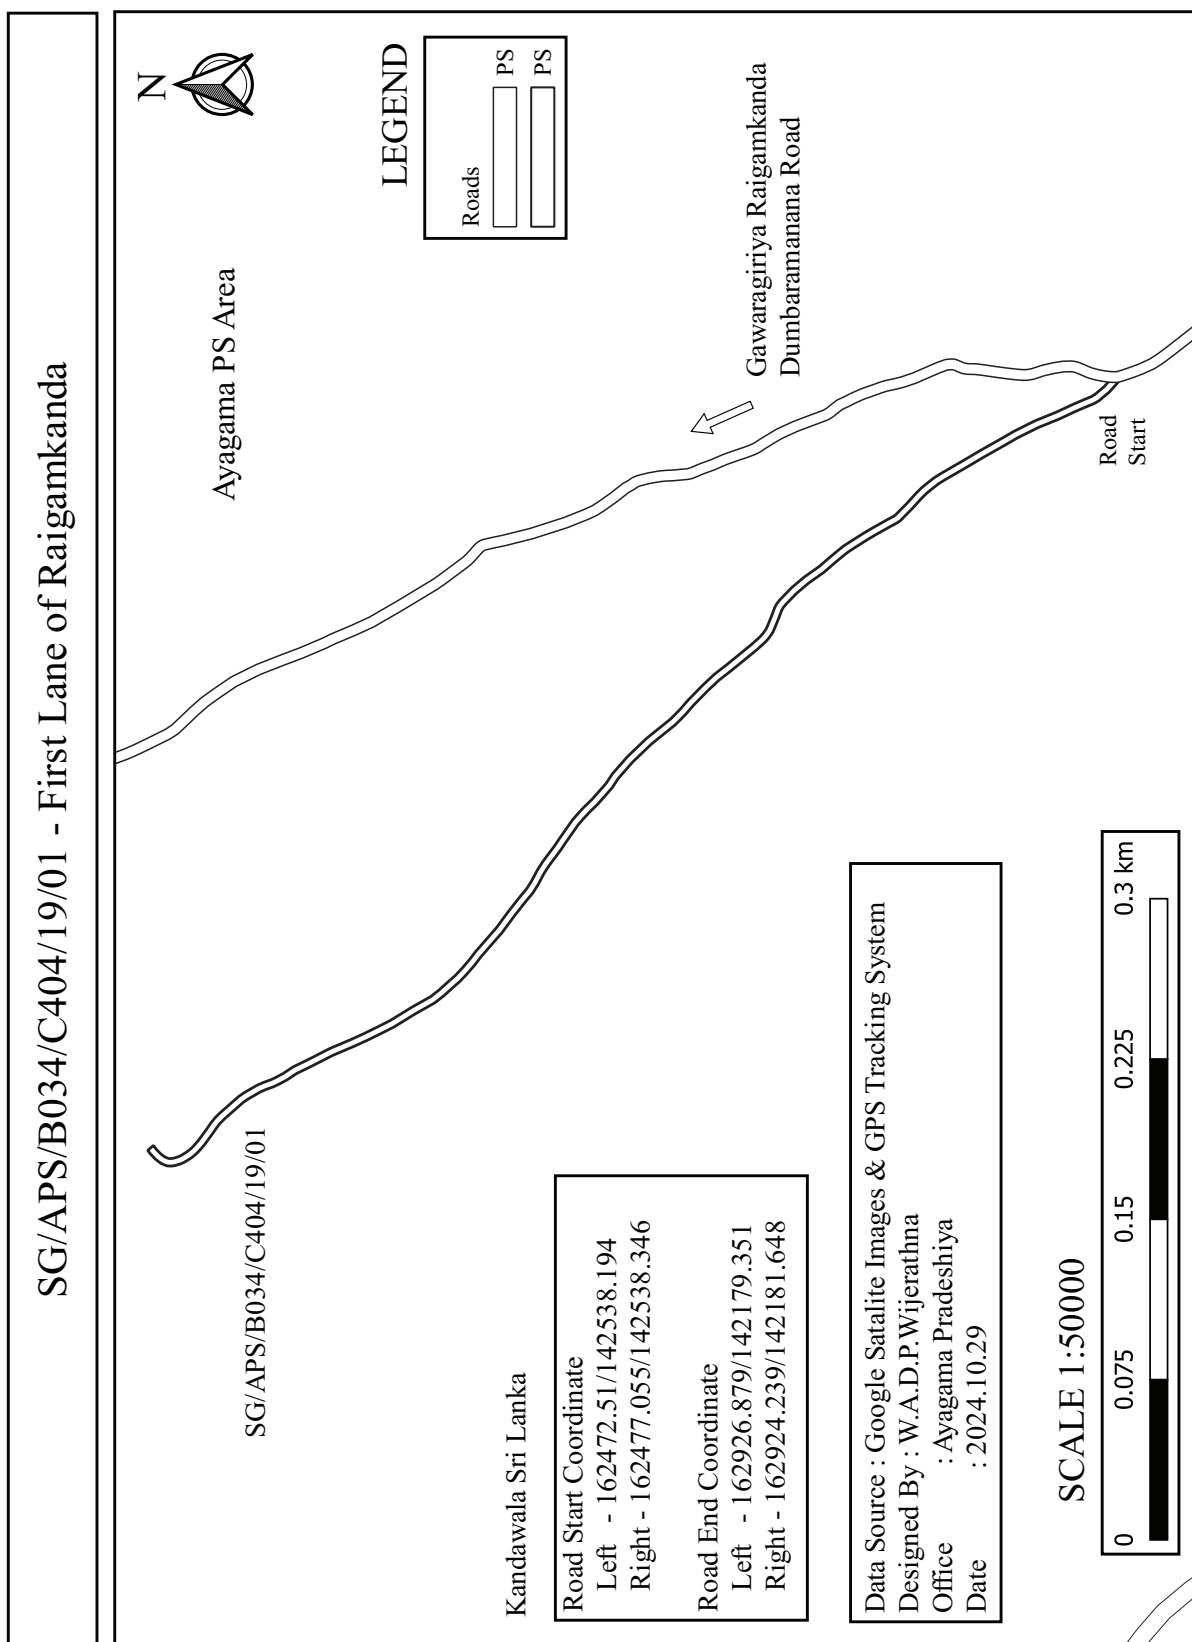


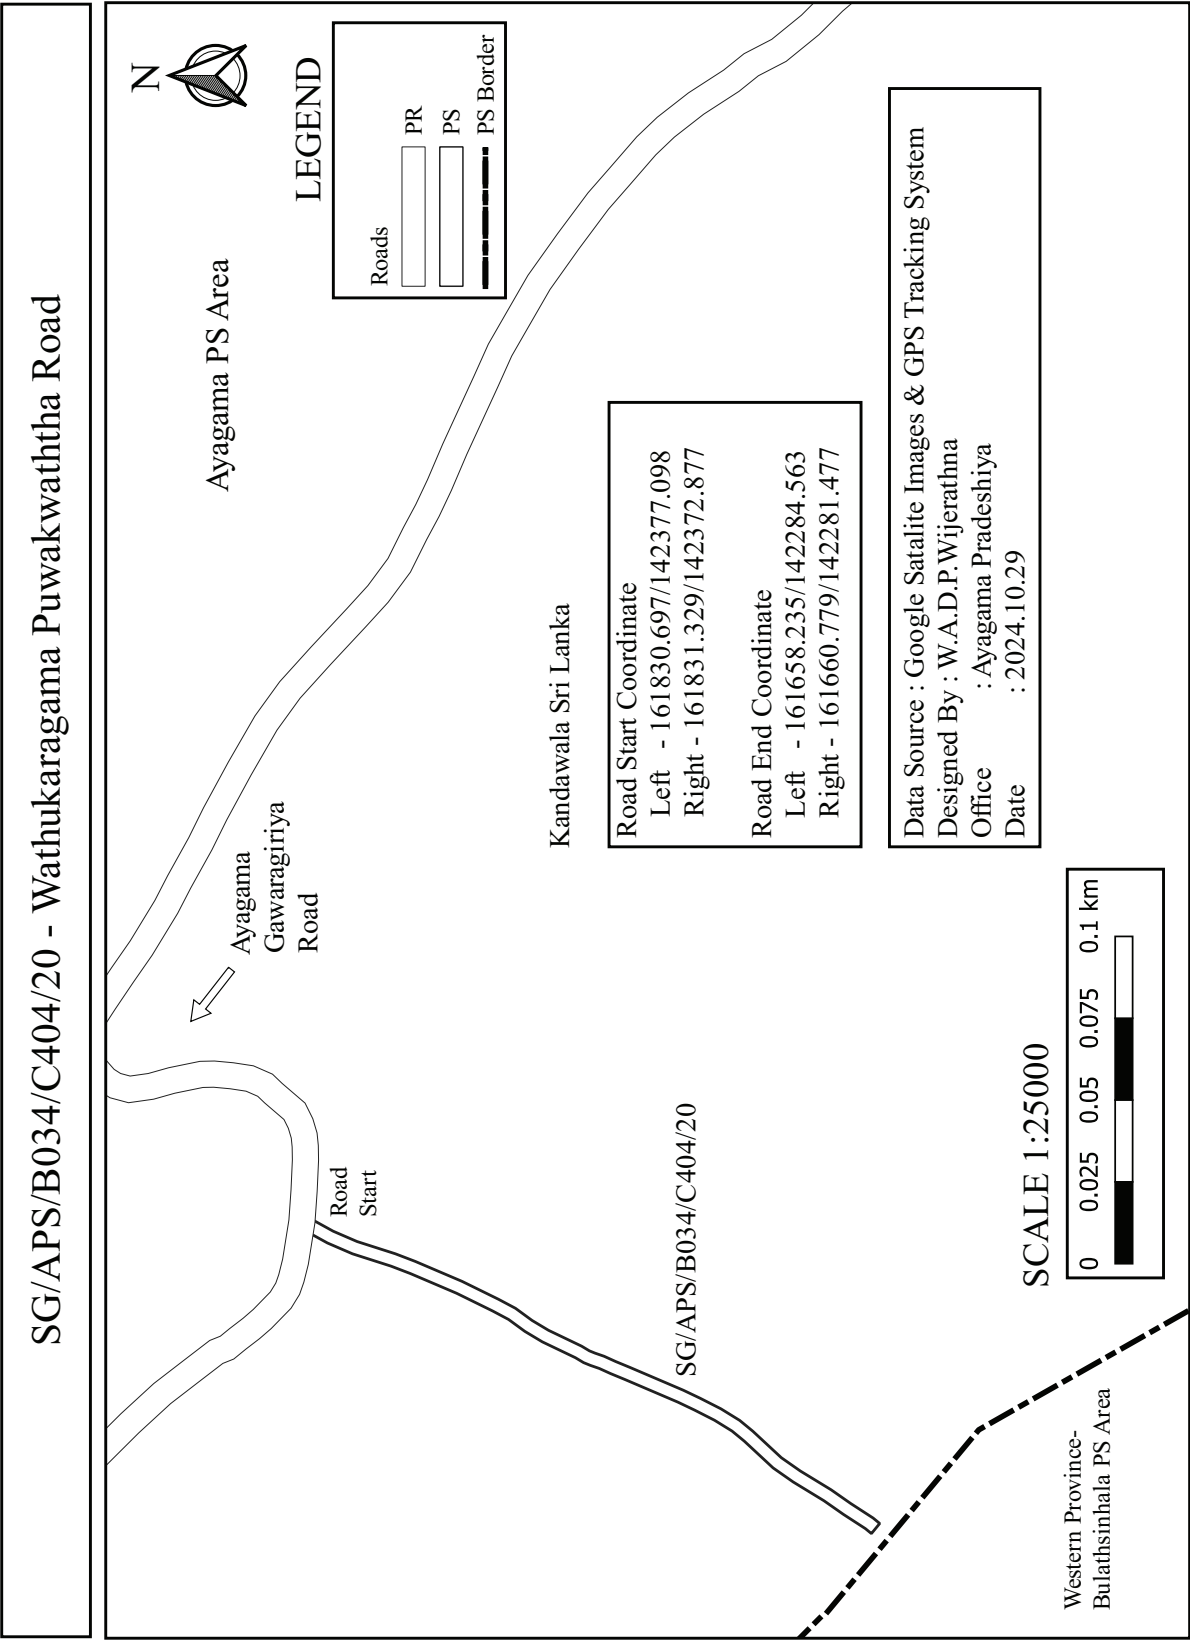



SG/APS/B034/C404/20/01 - Wathukaragama Galwaththa Road

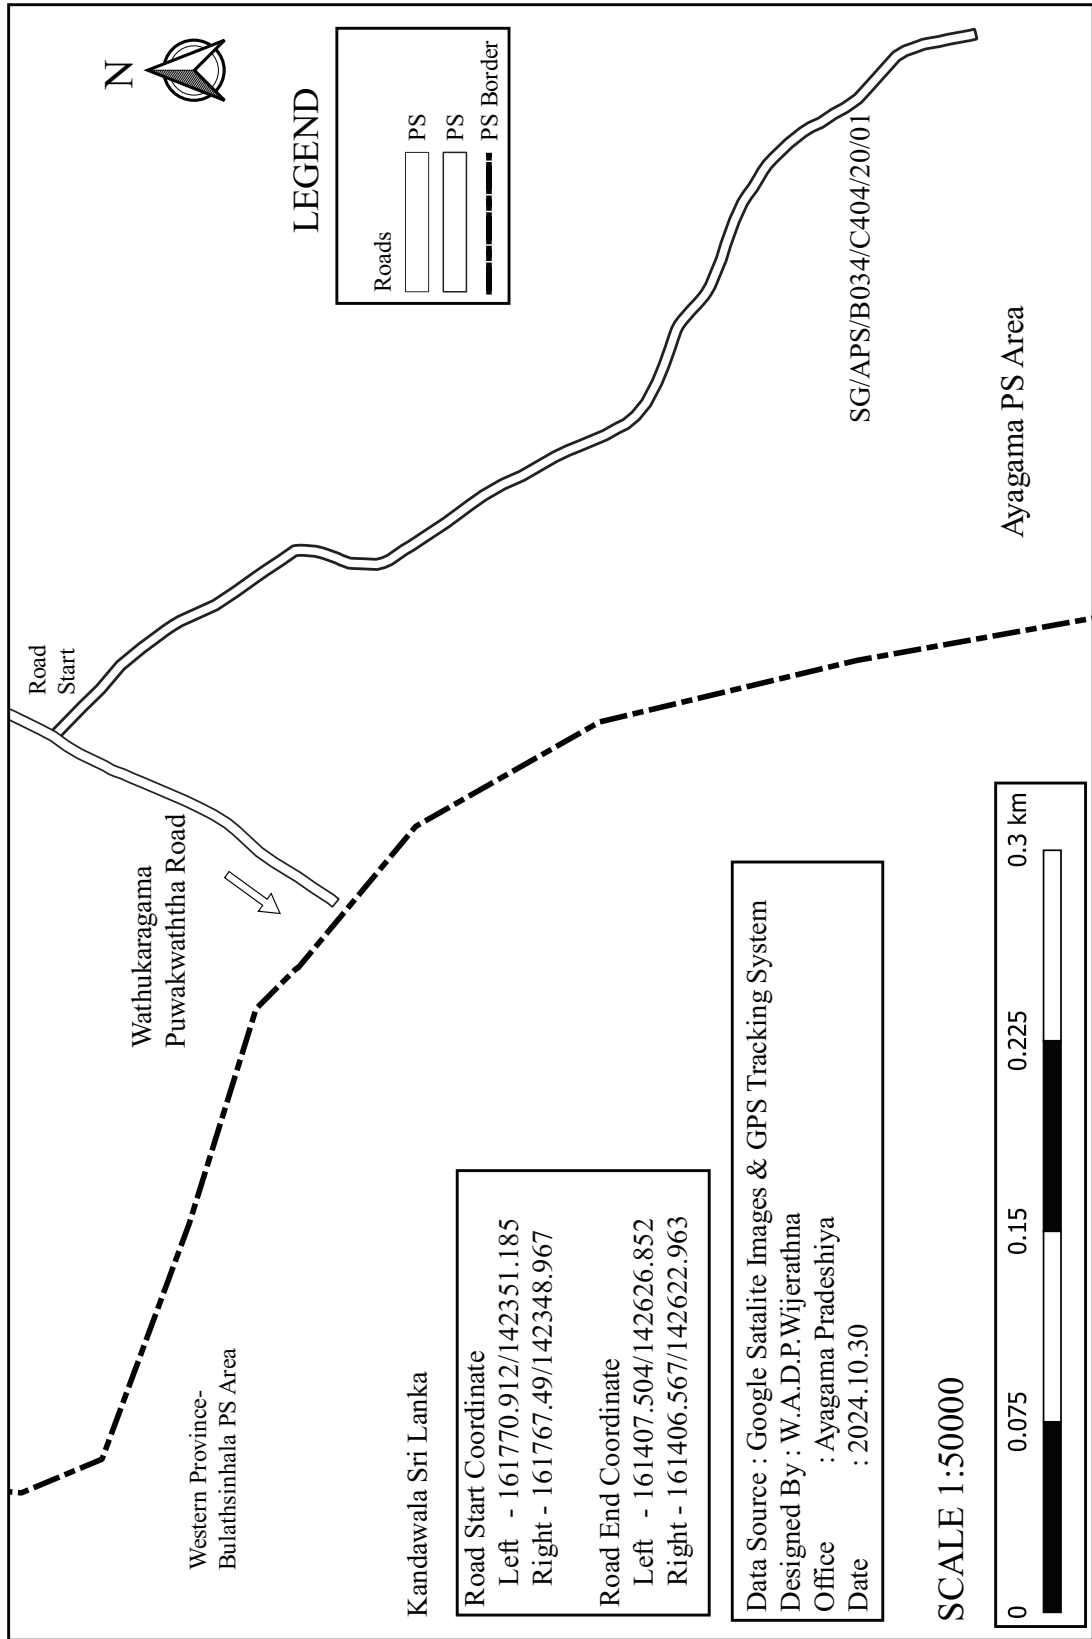


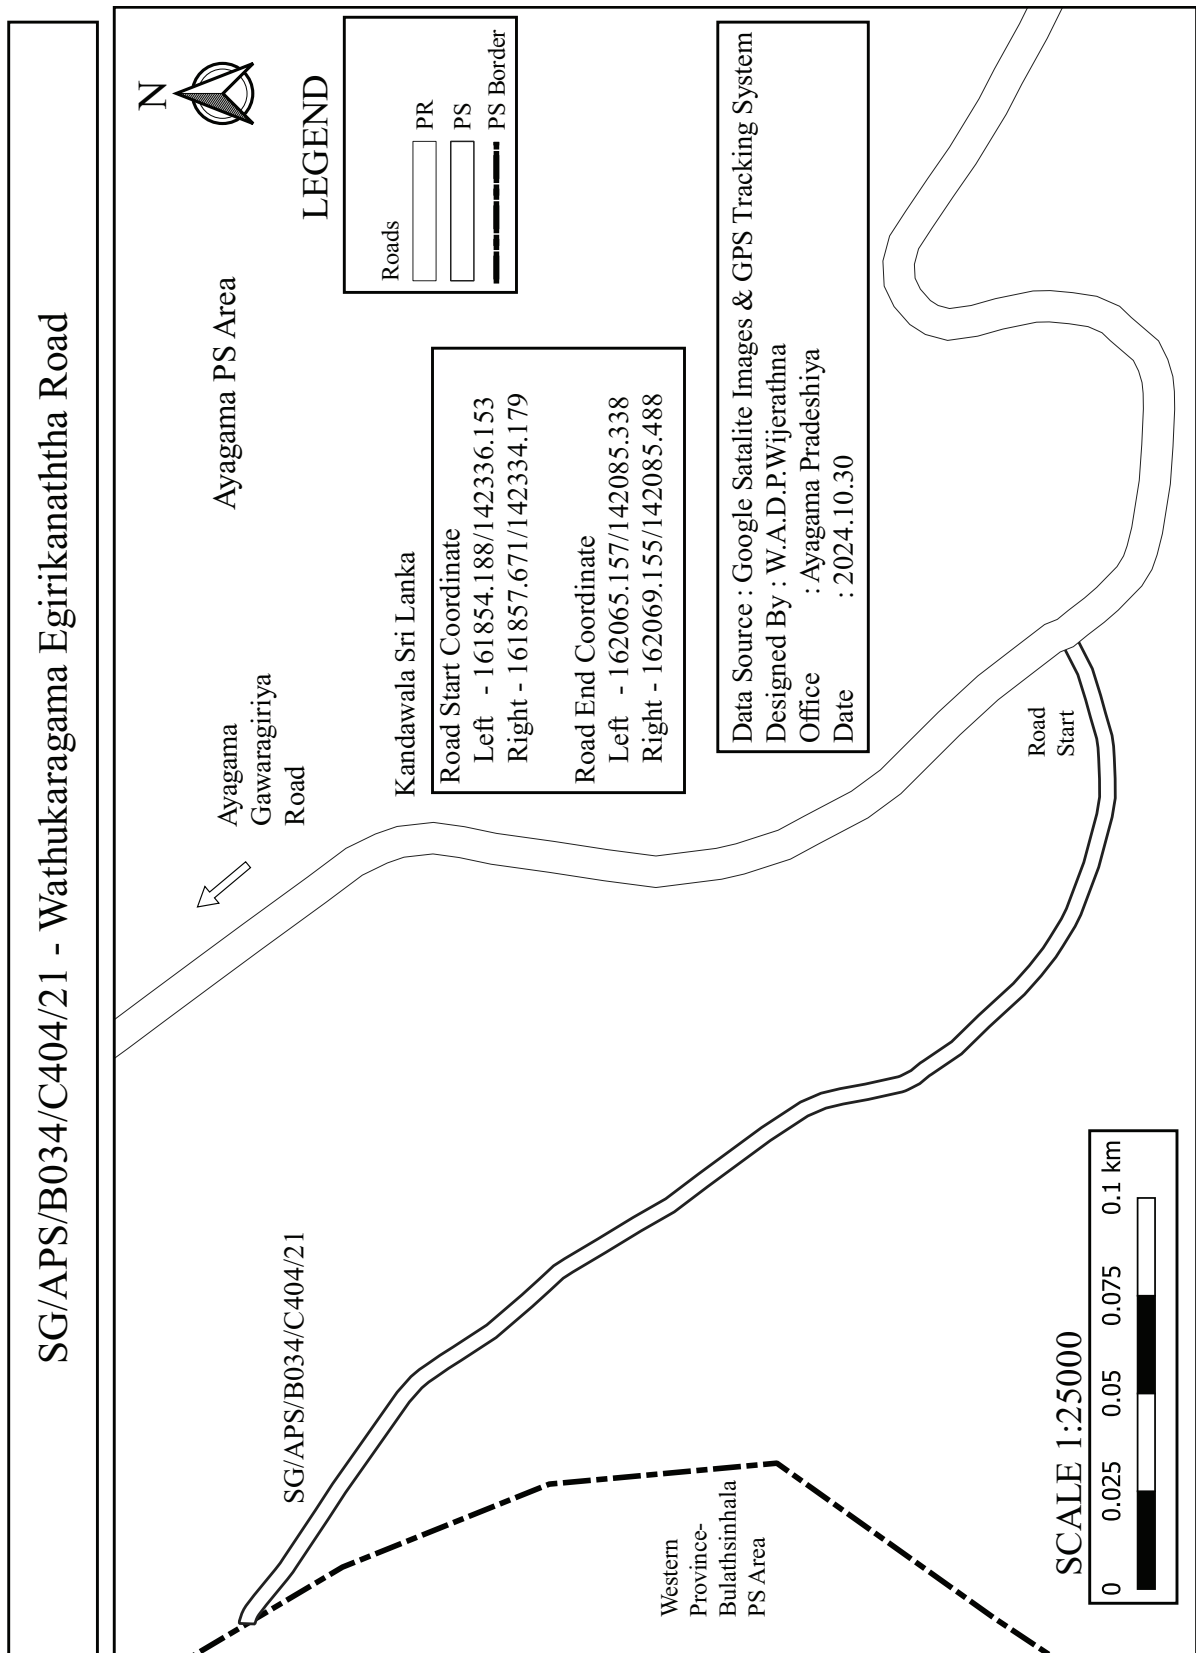


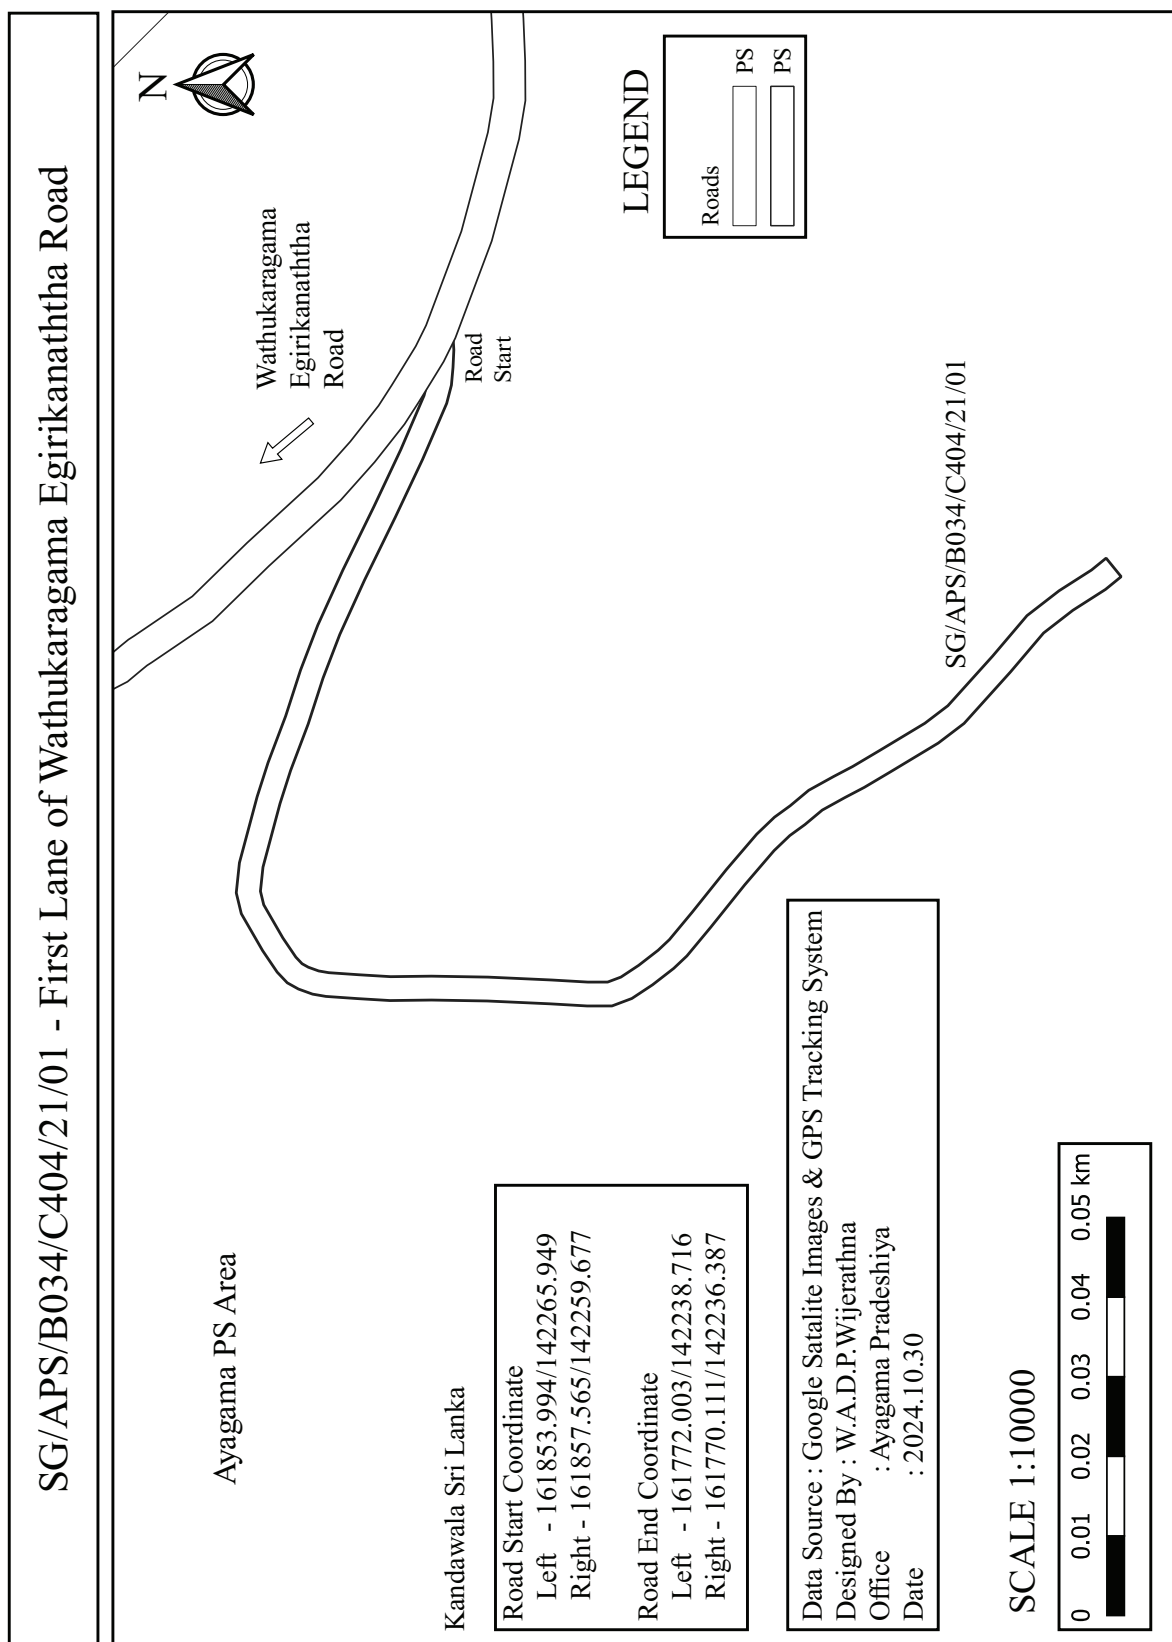


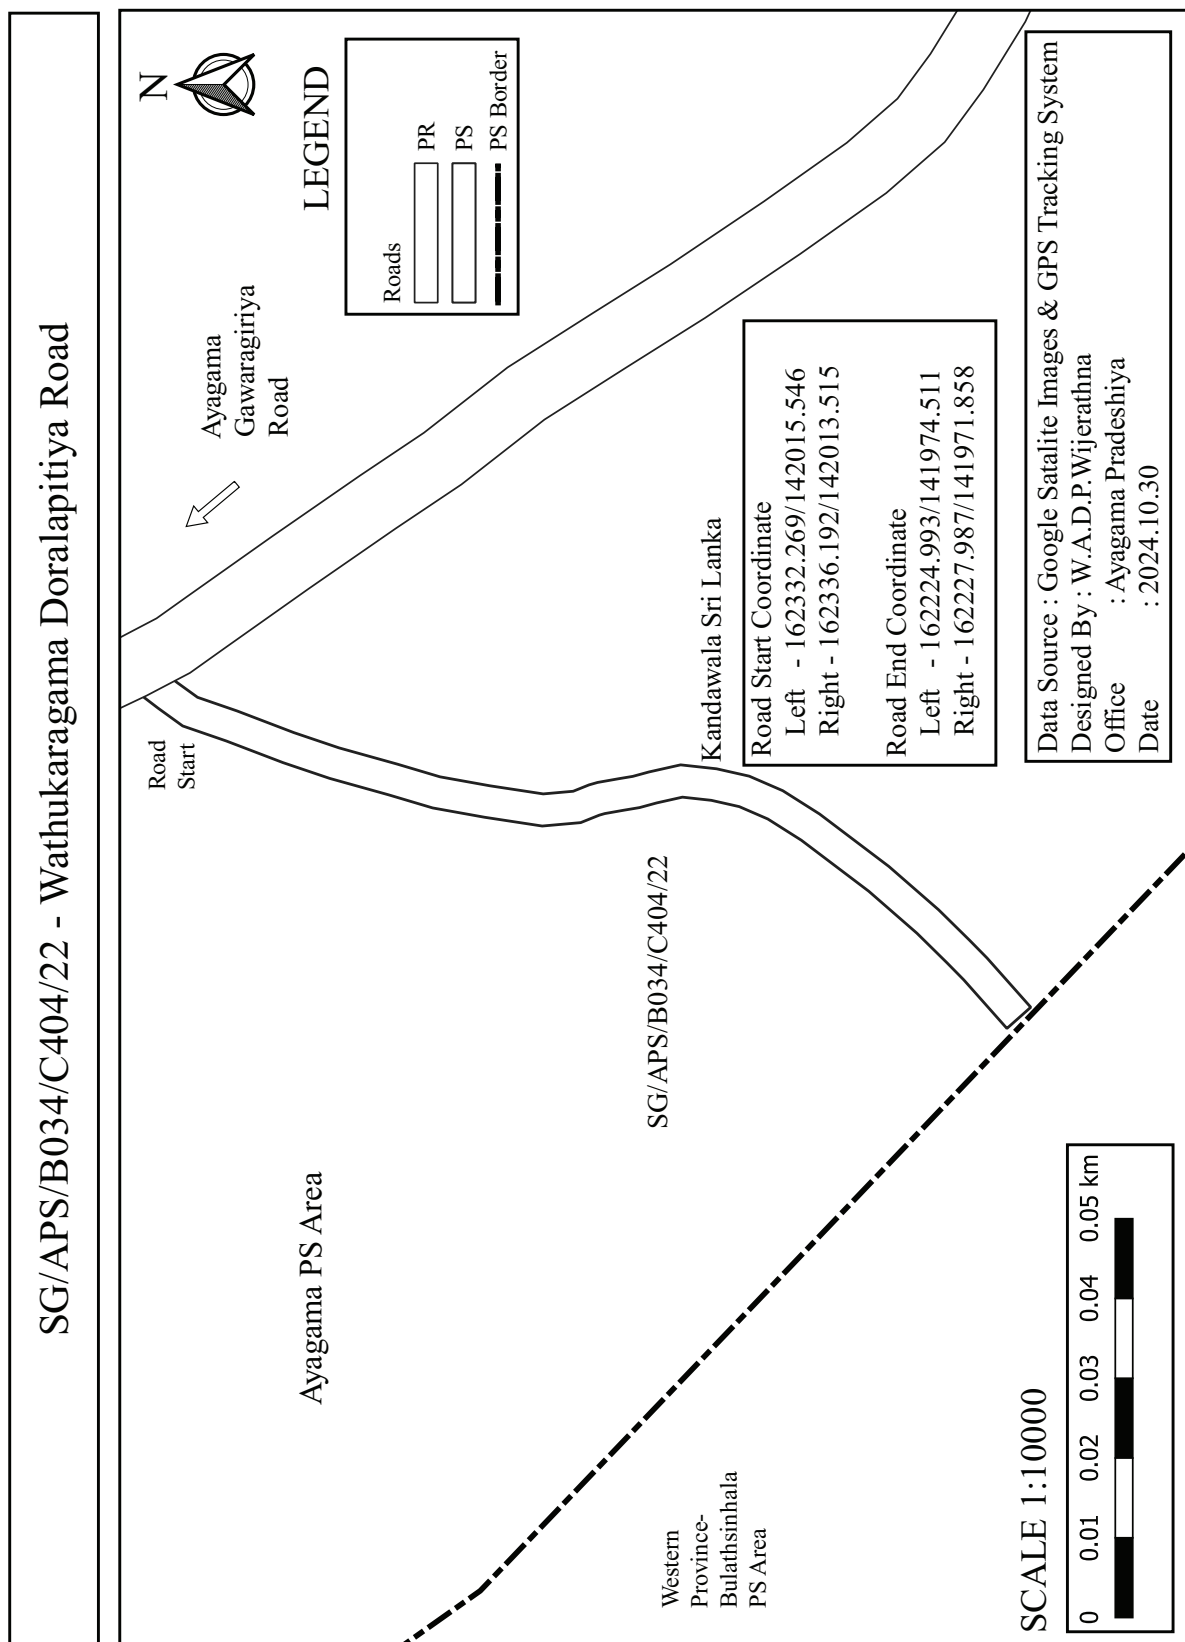


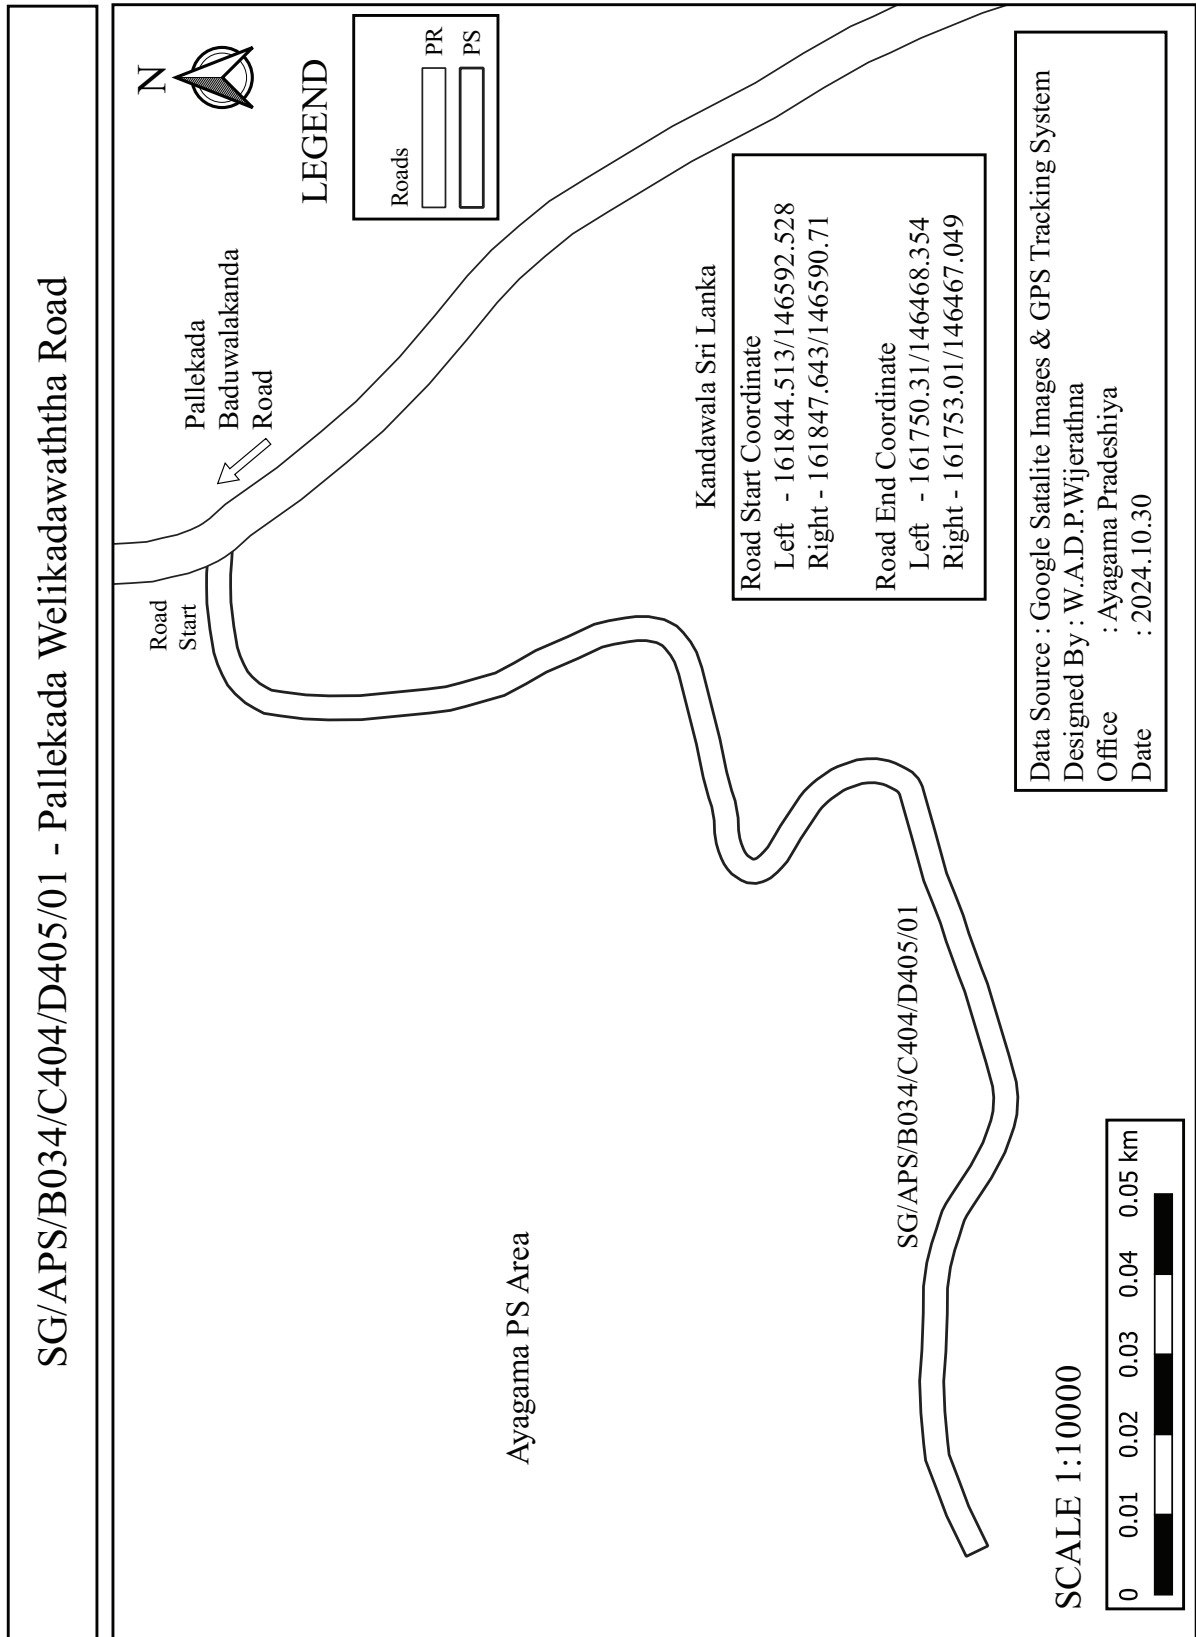


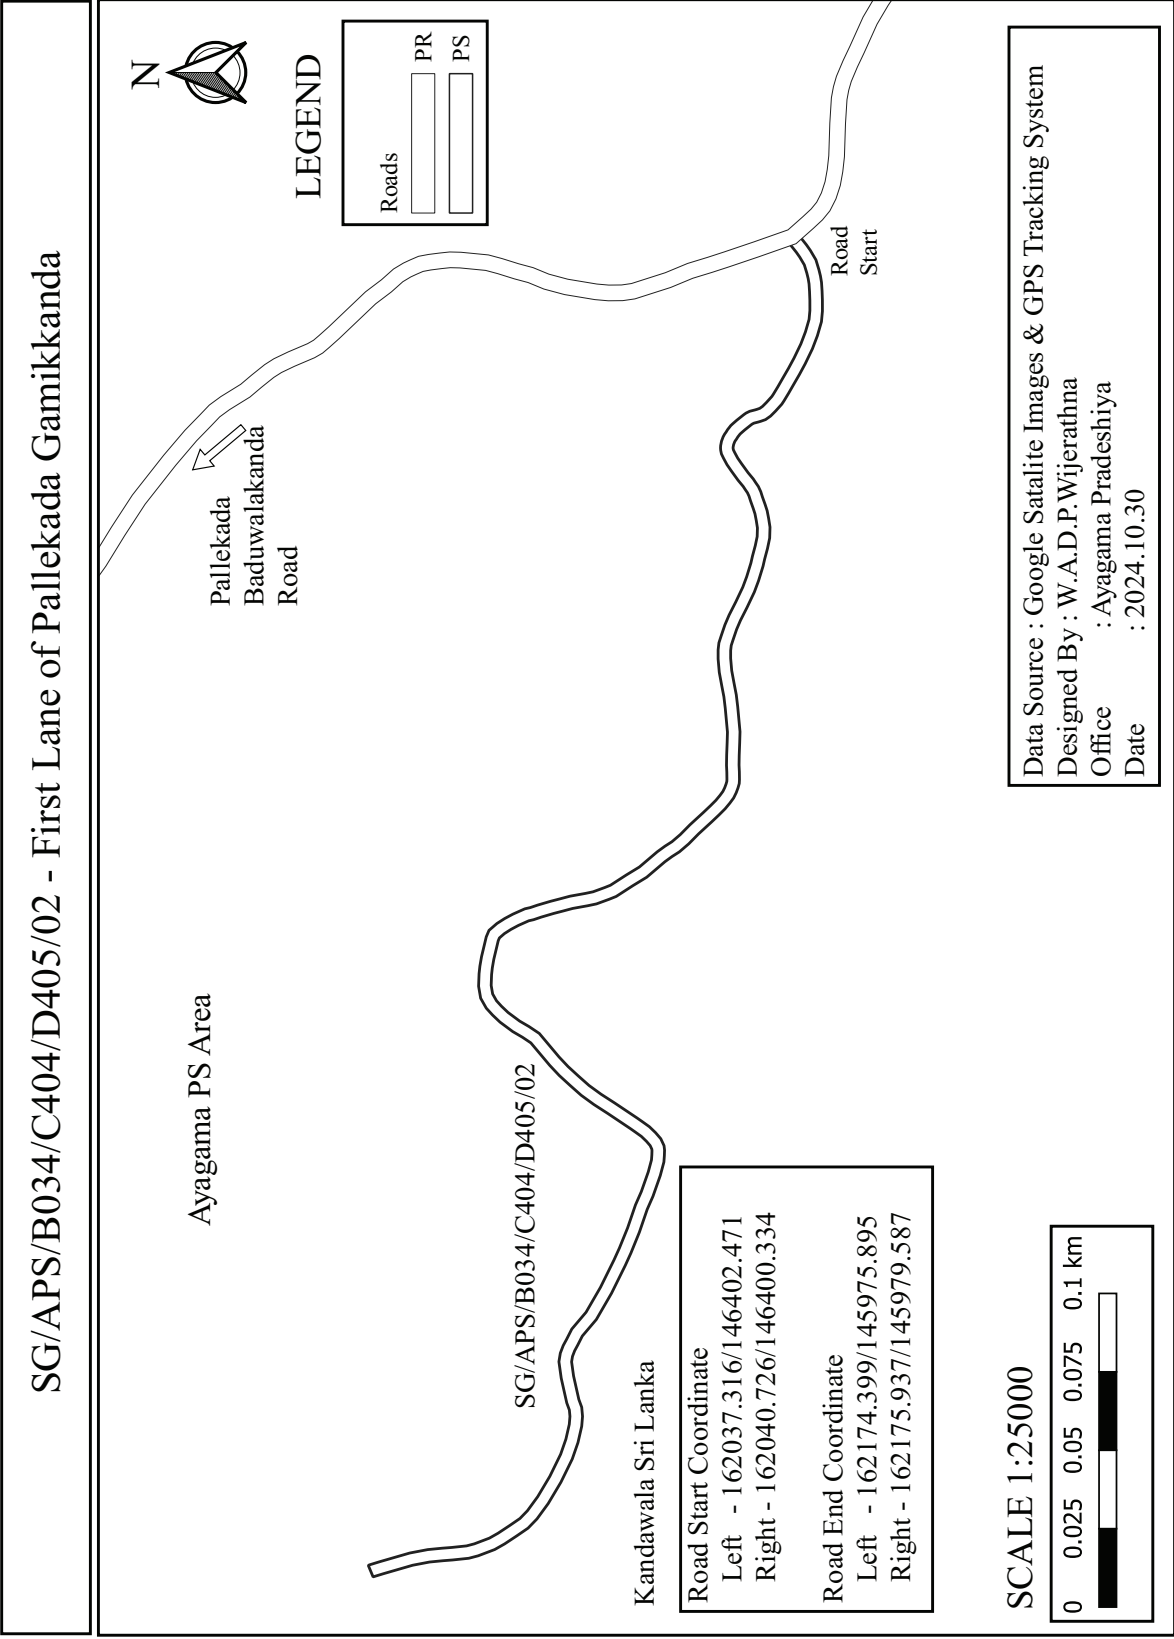


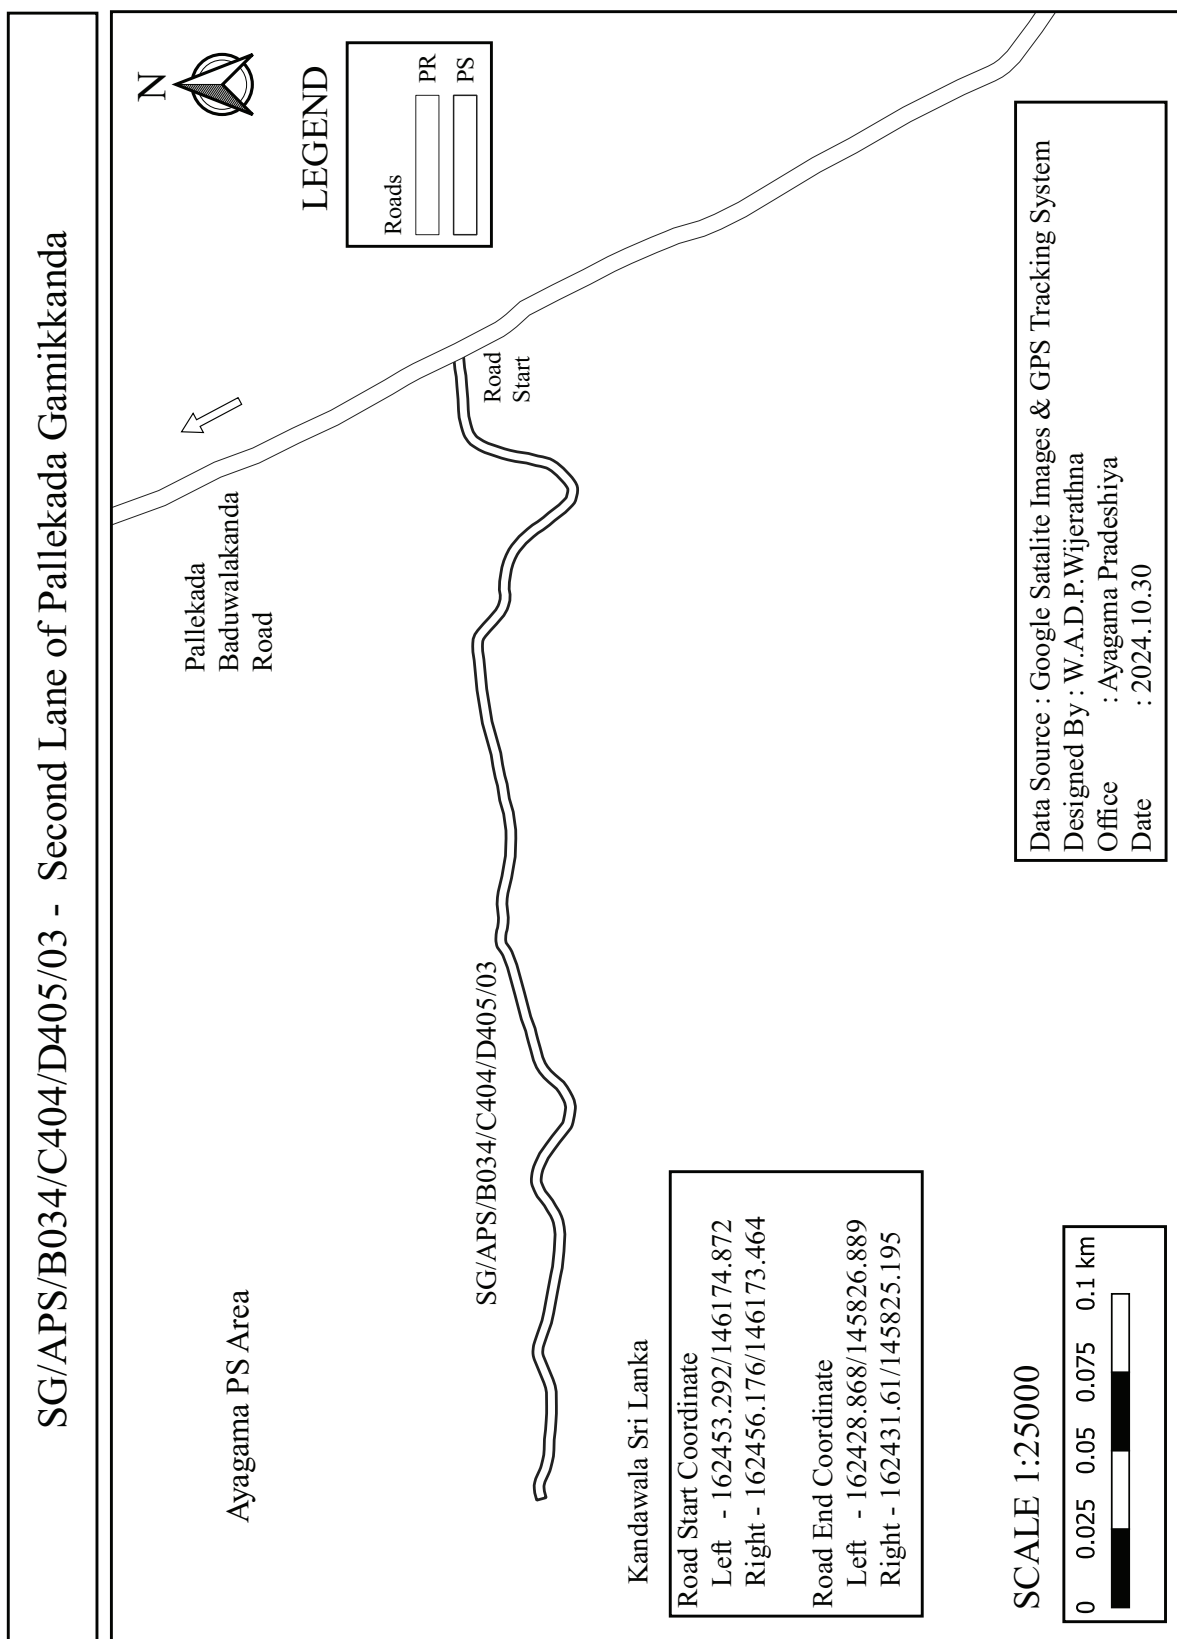


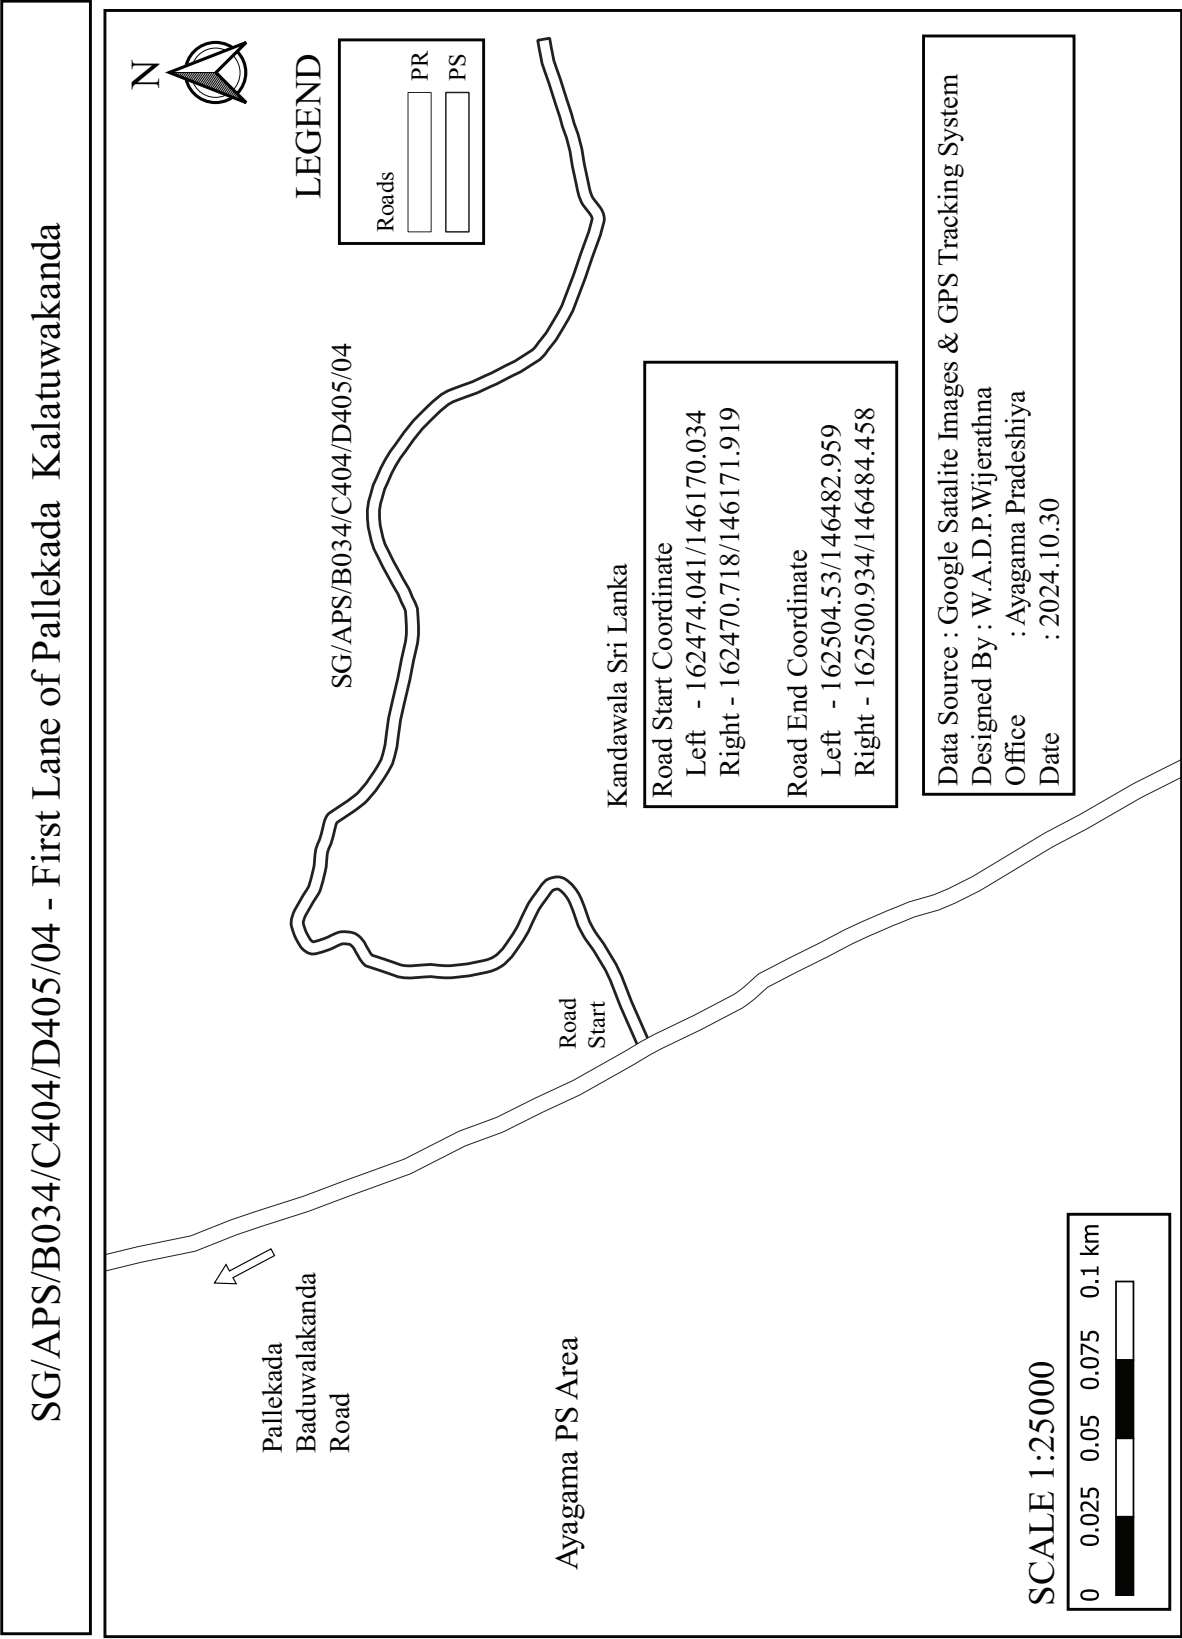


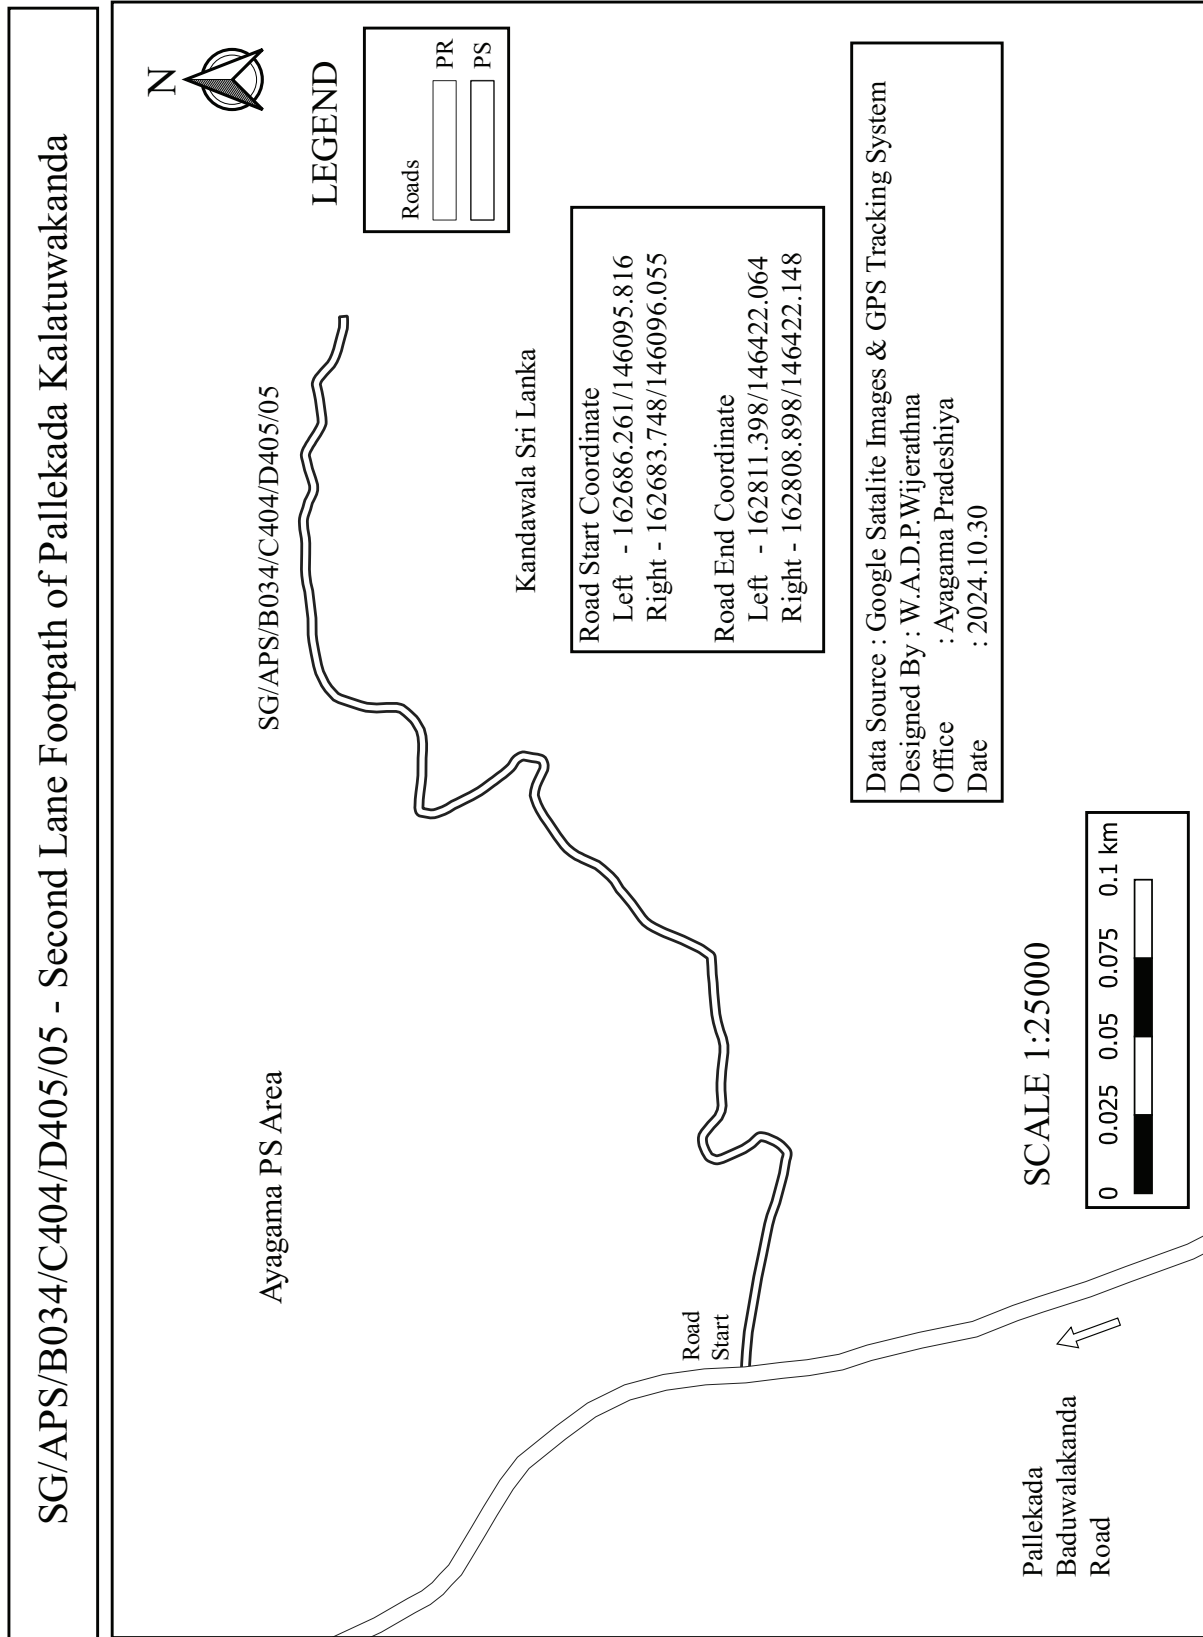


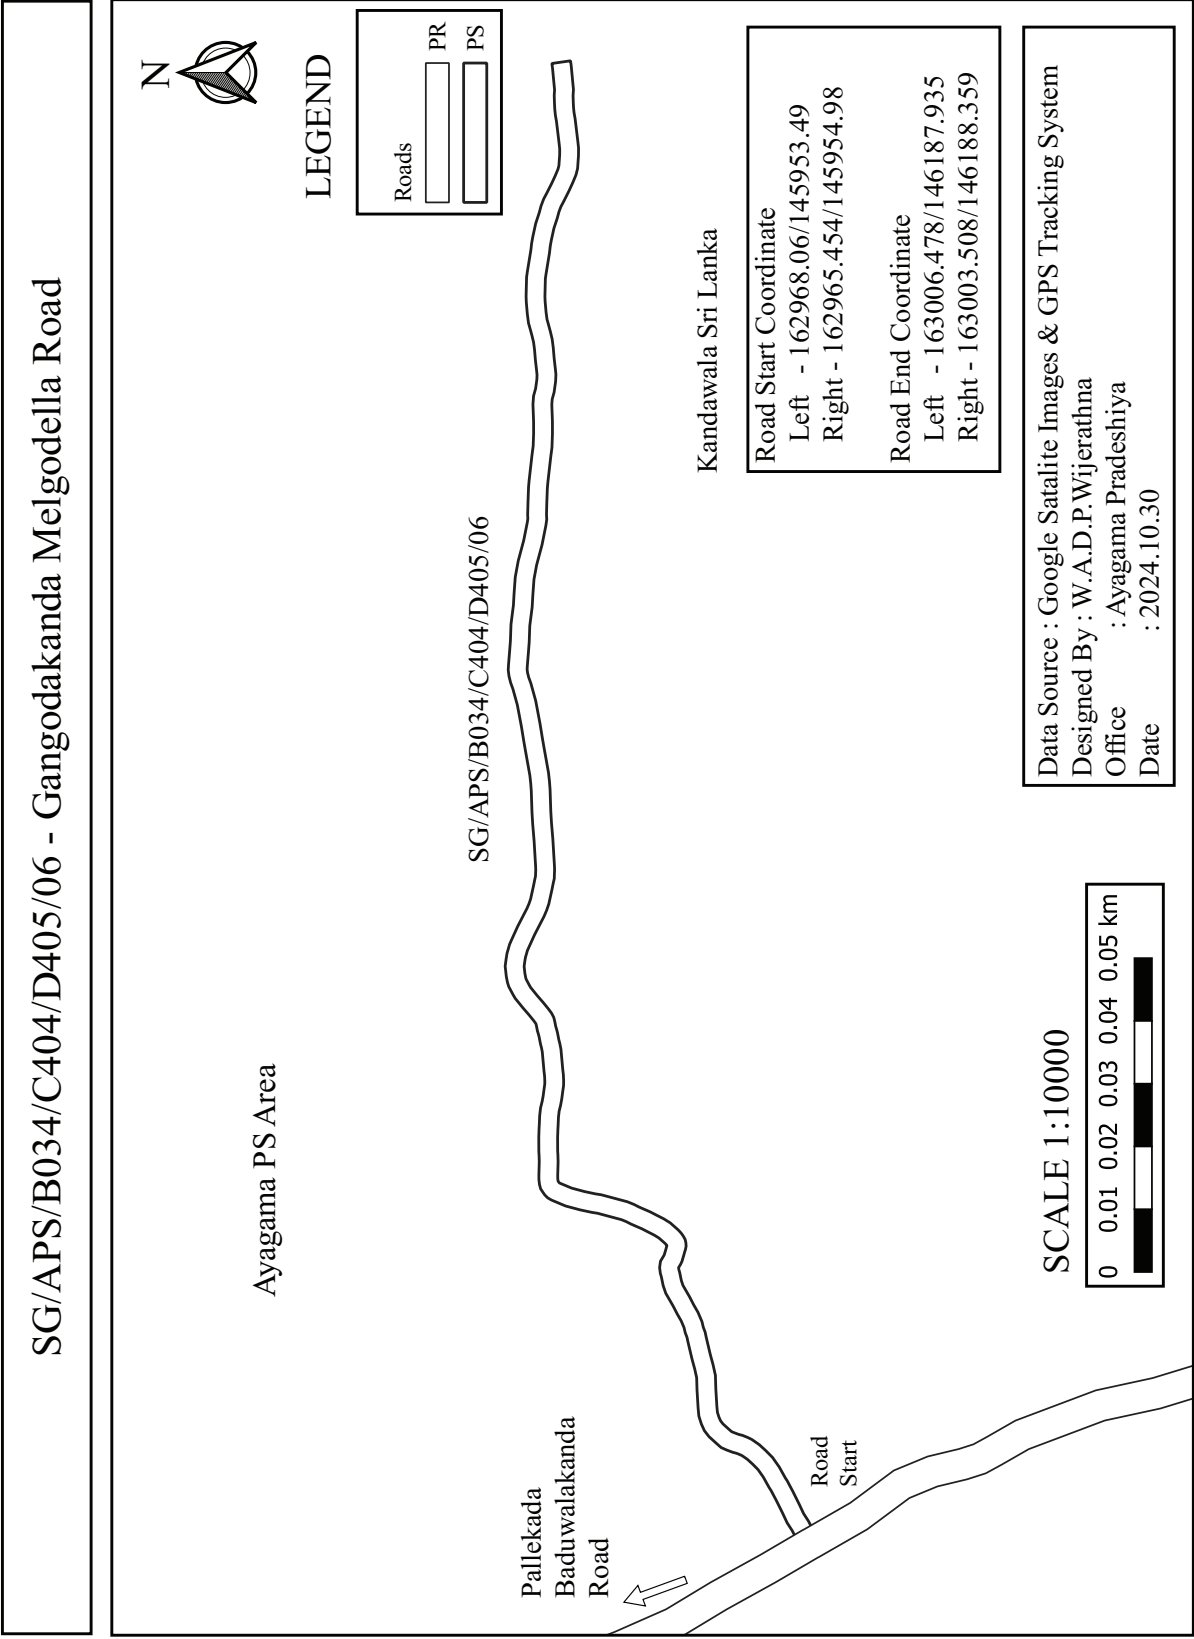


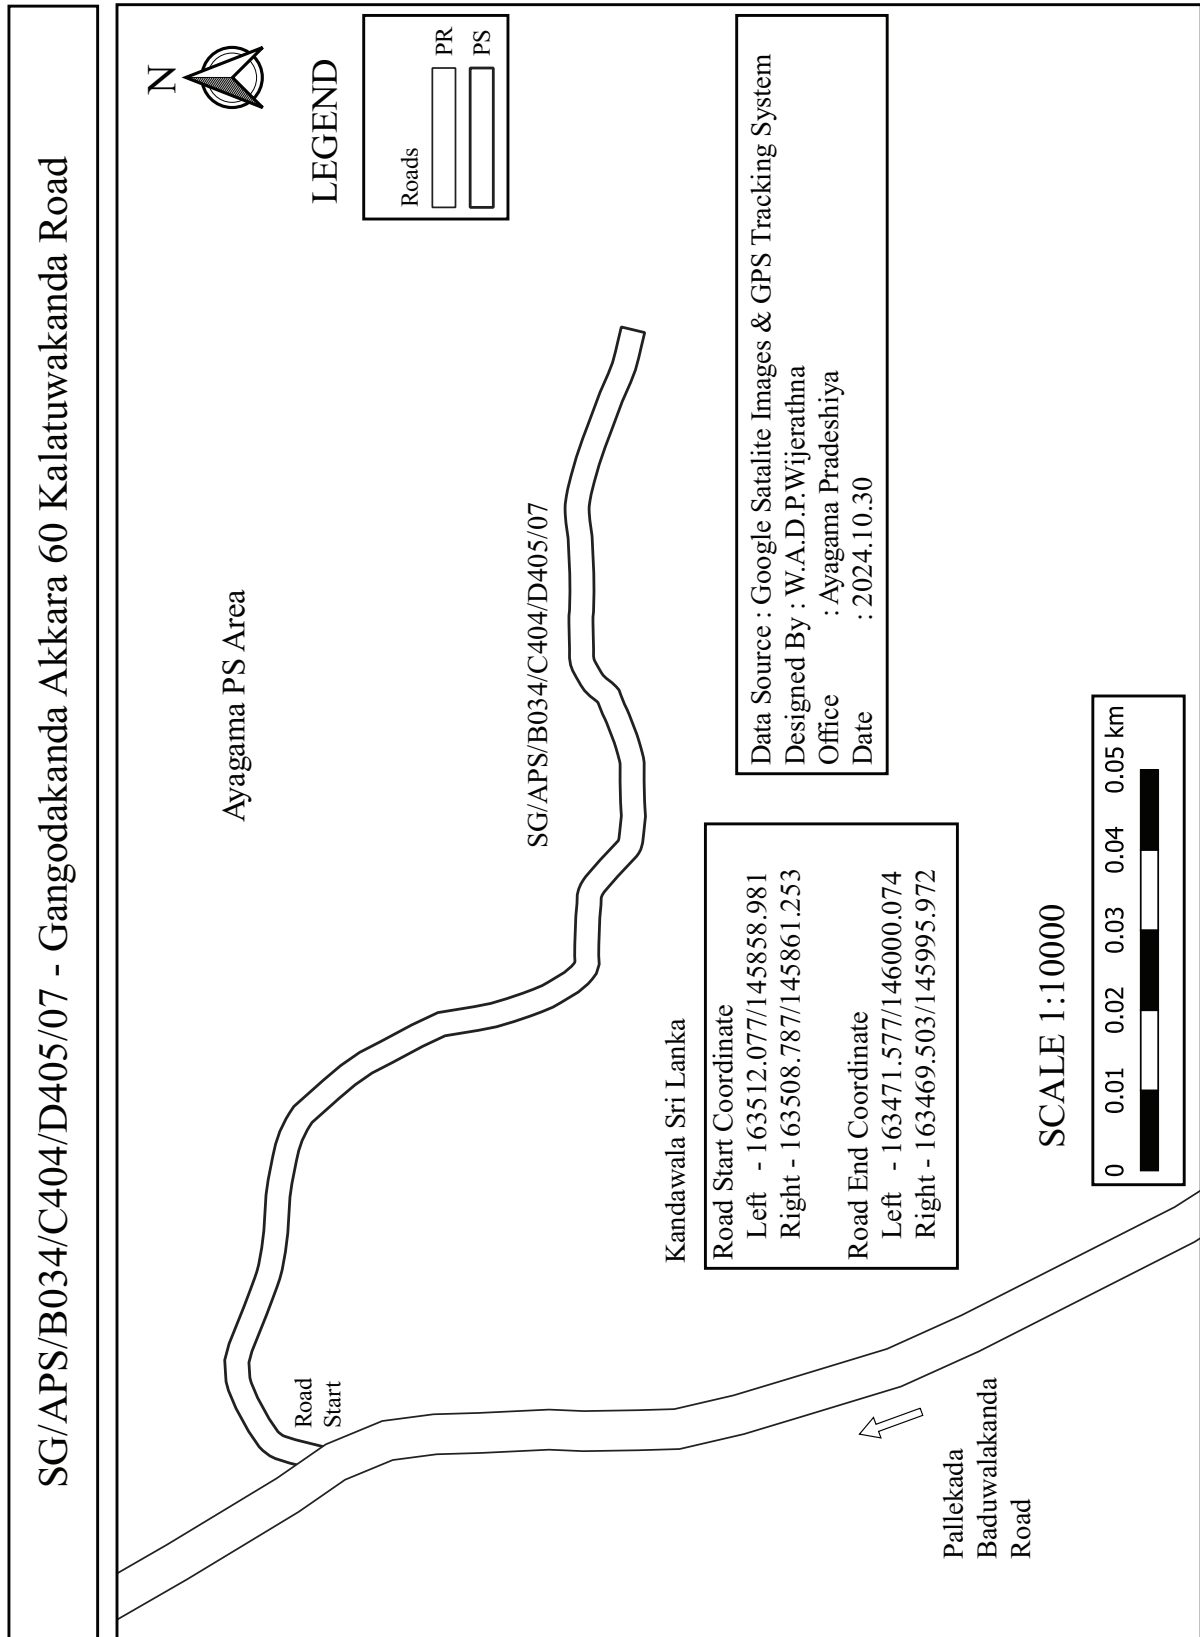


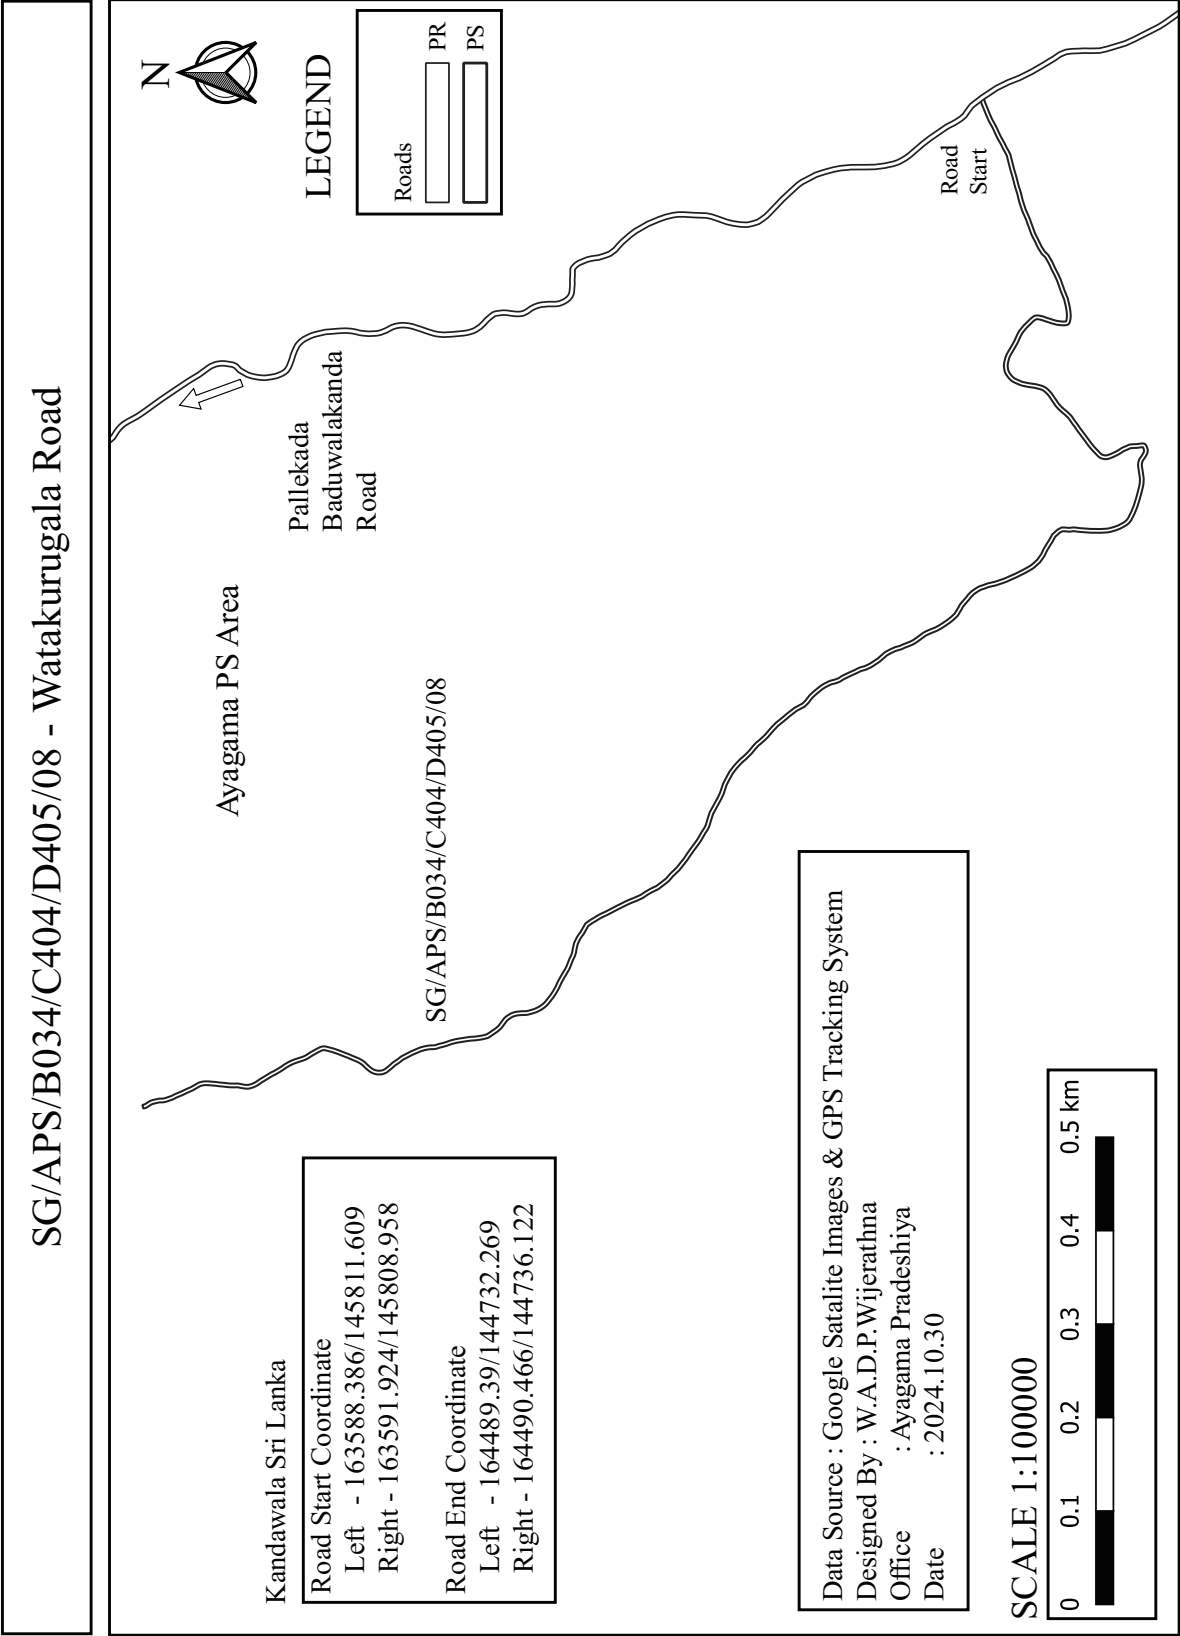

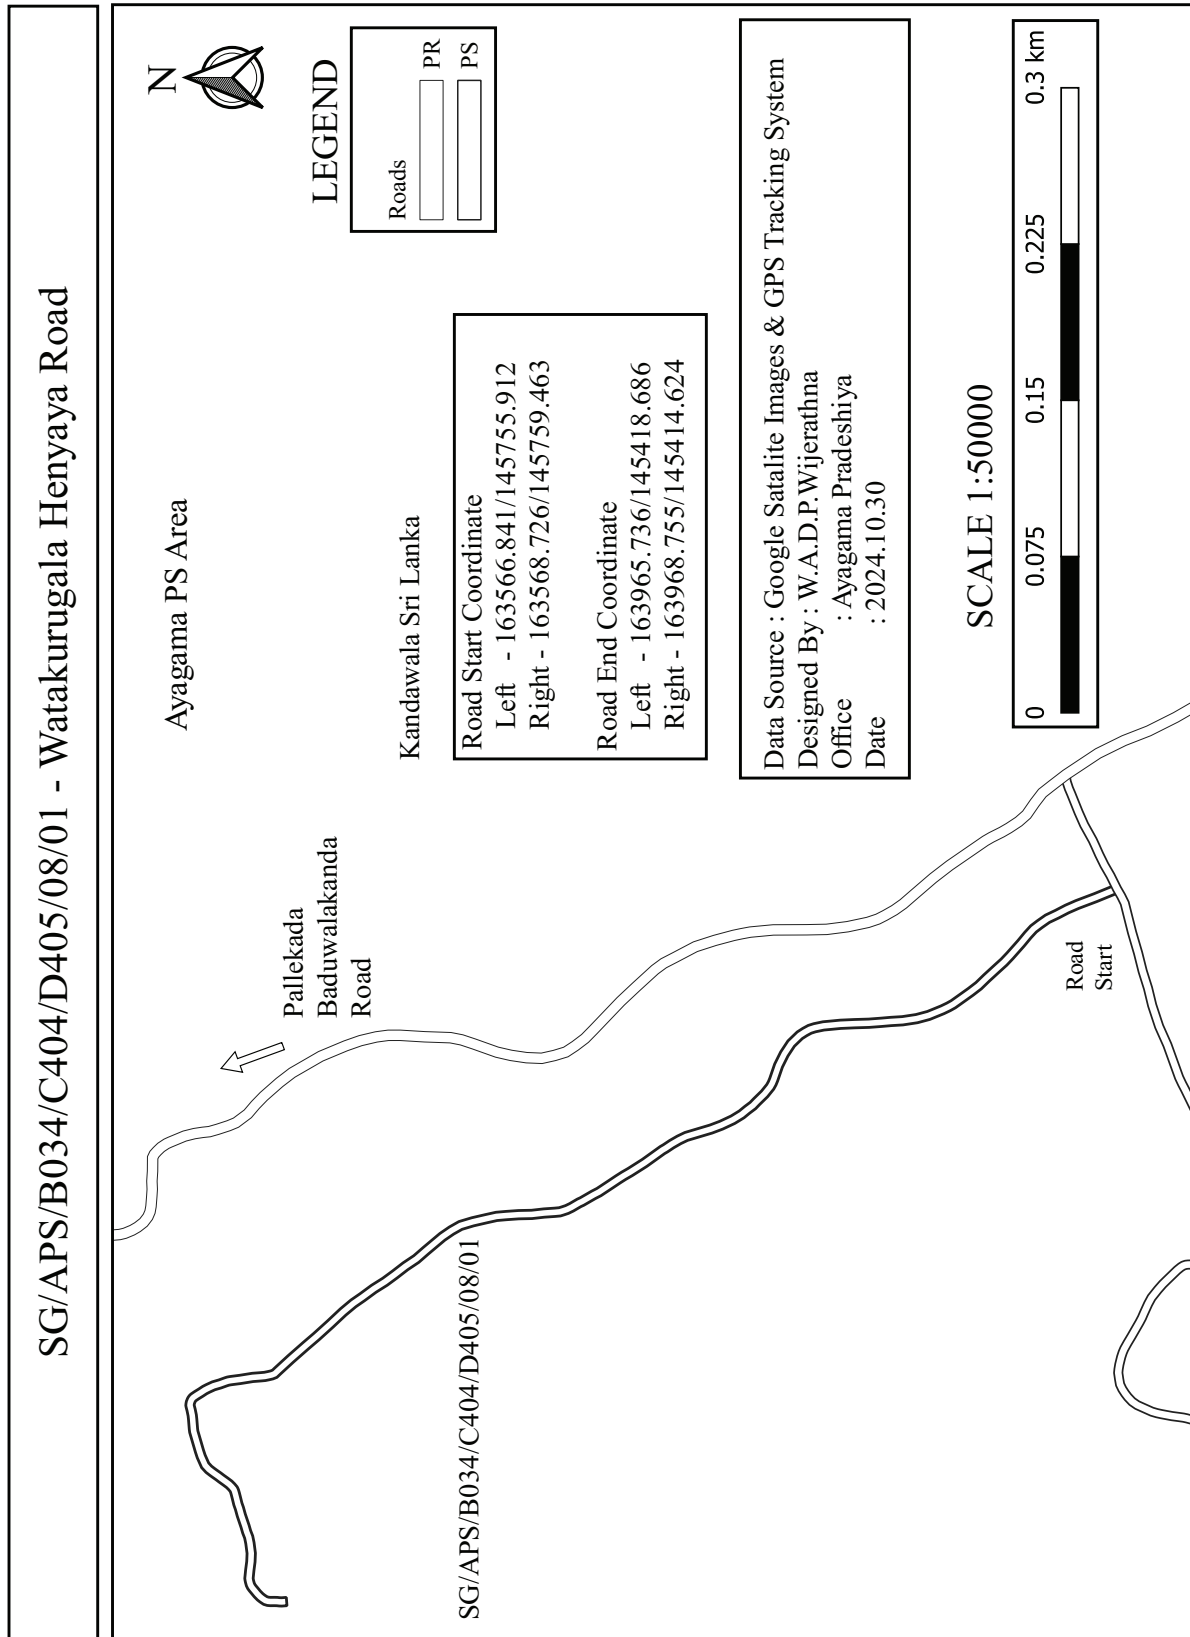


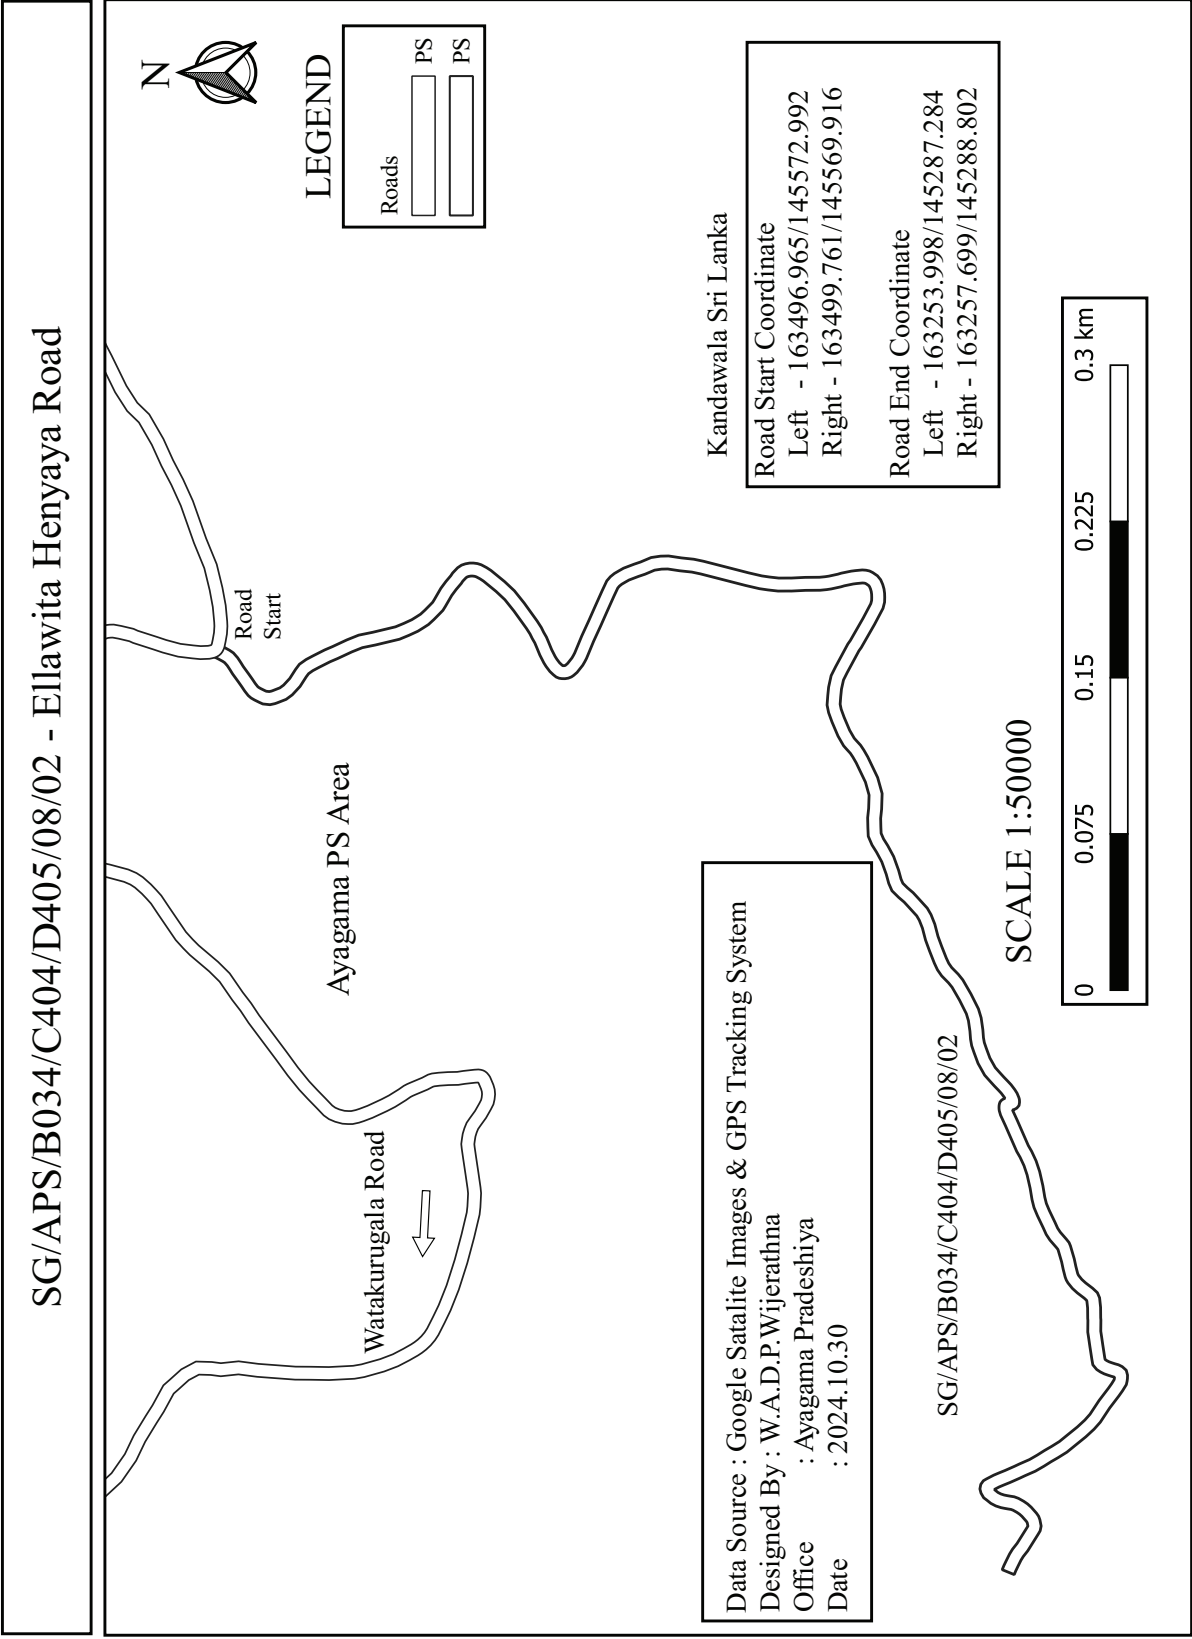


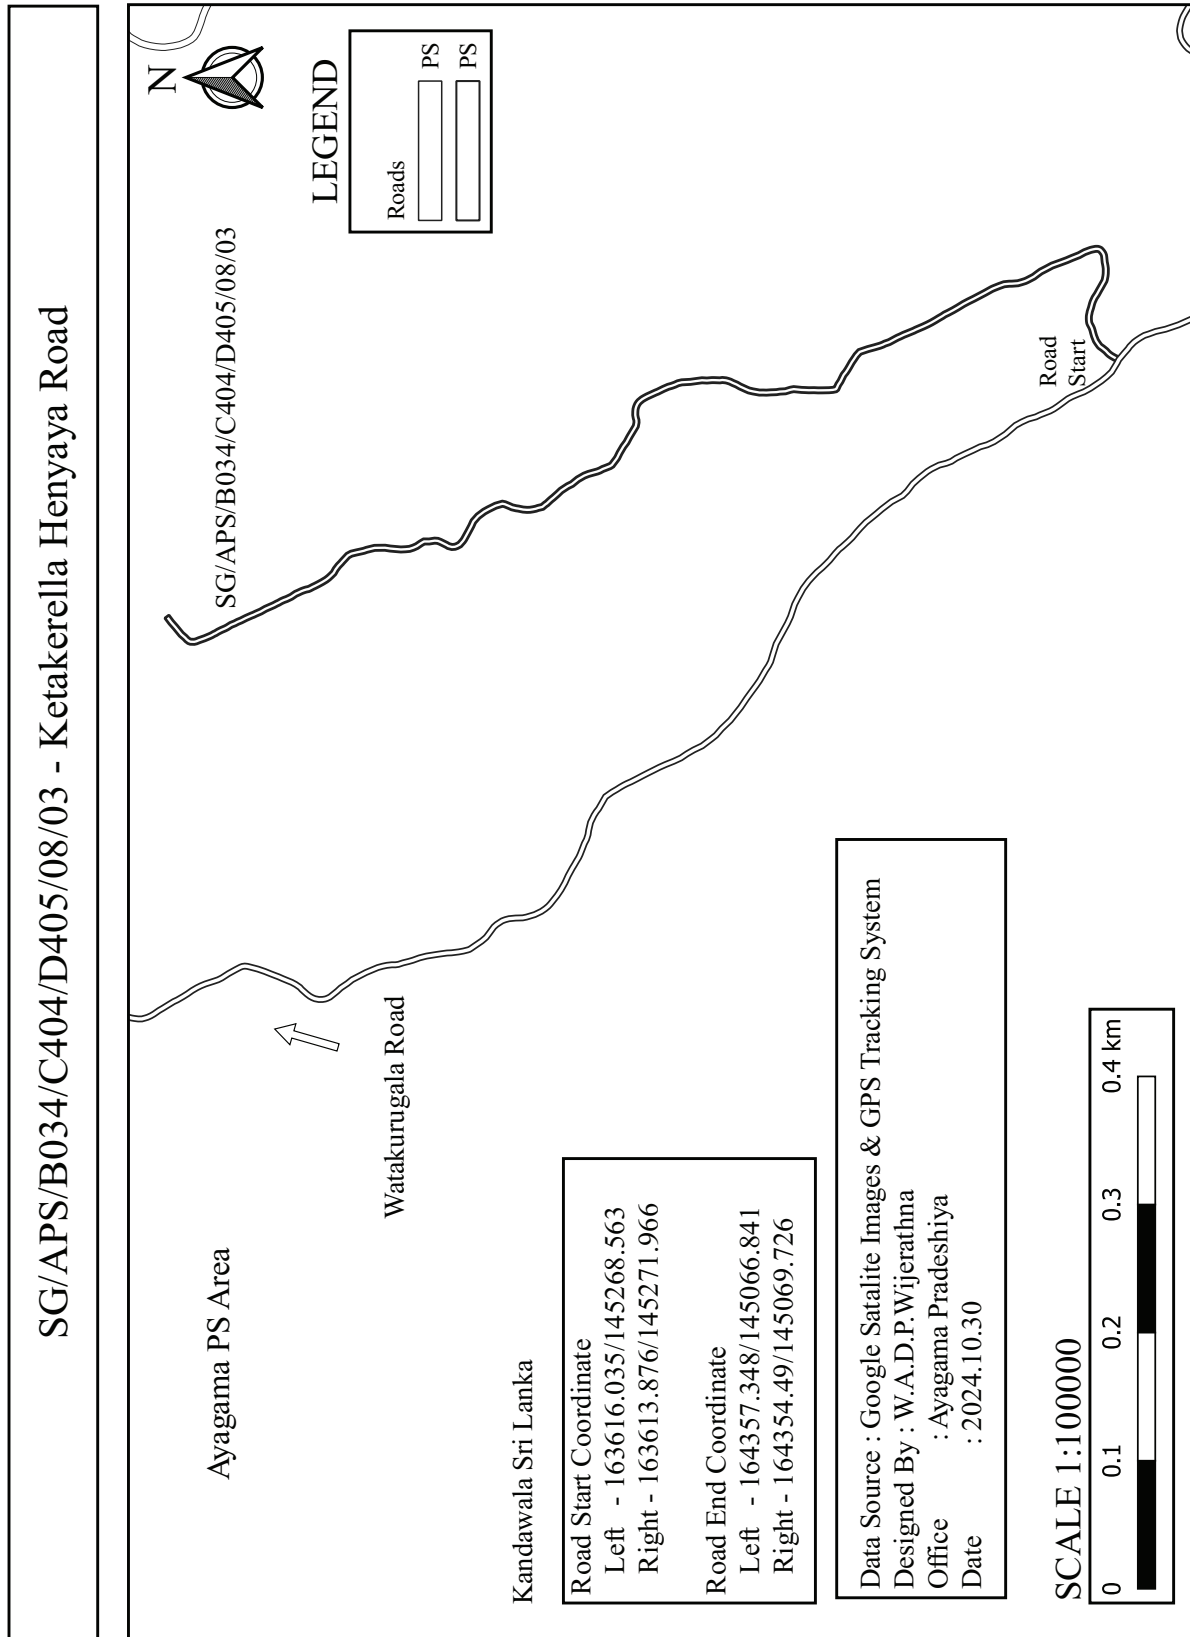


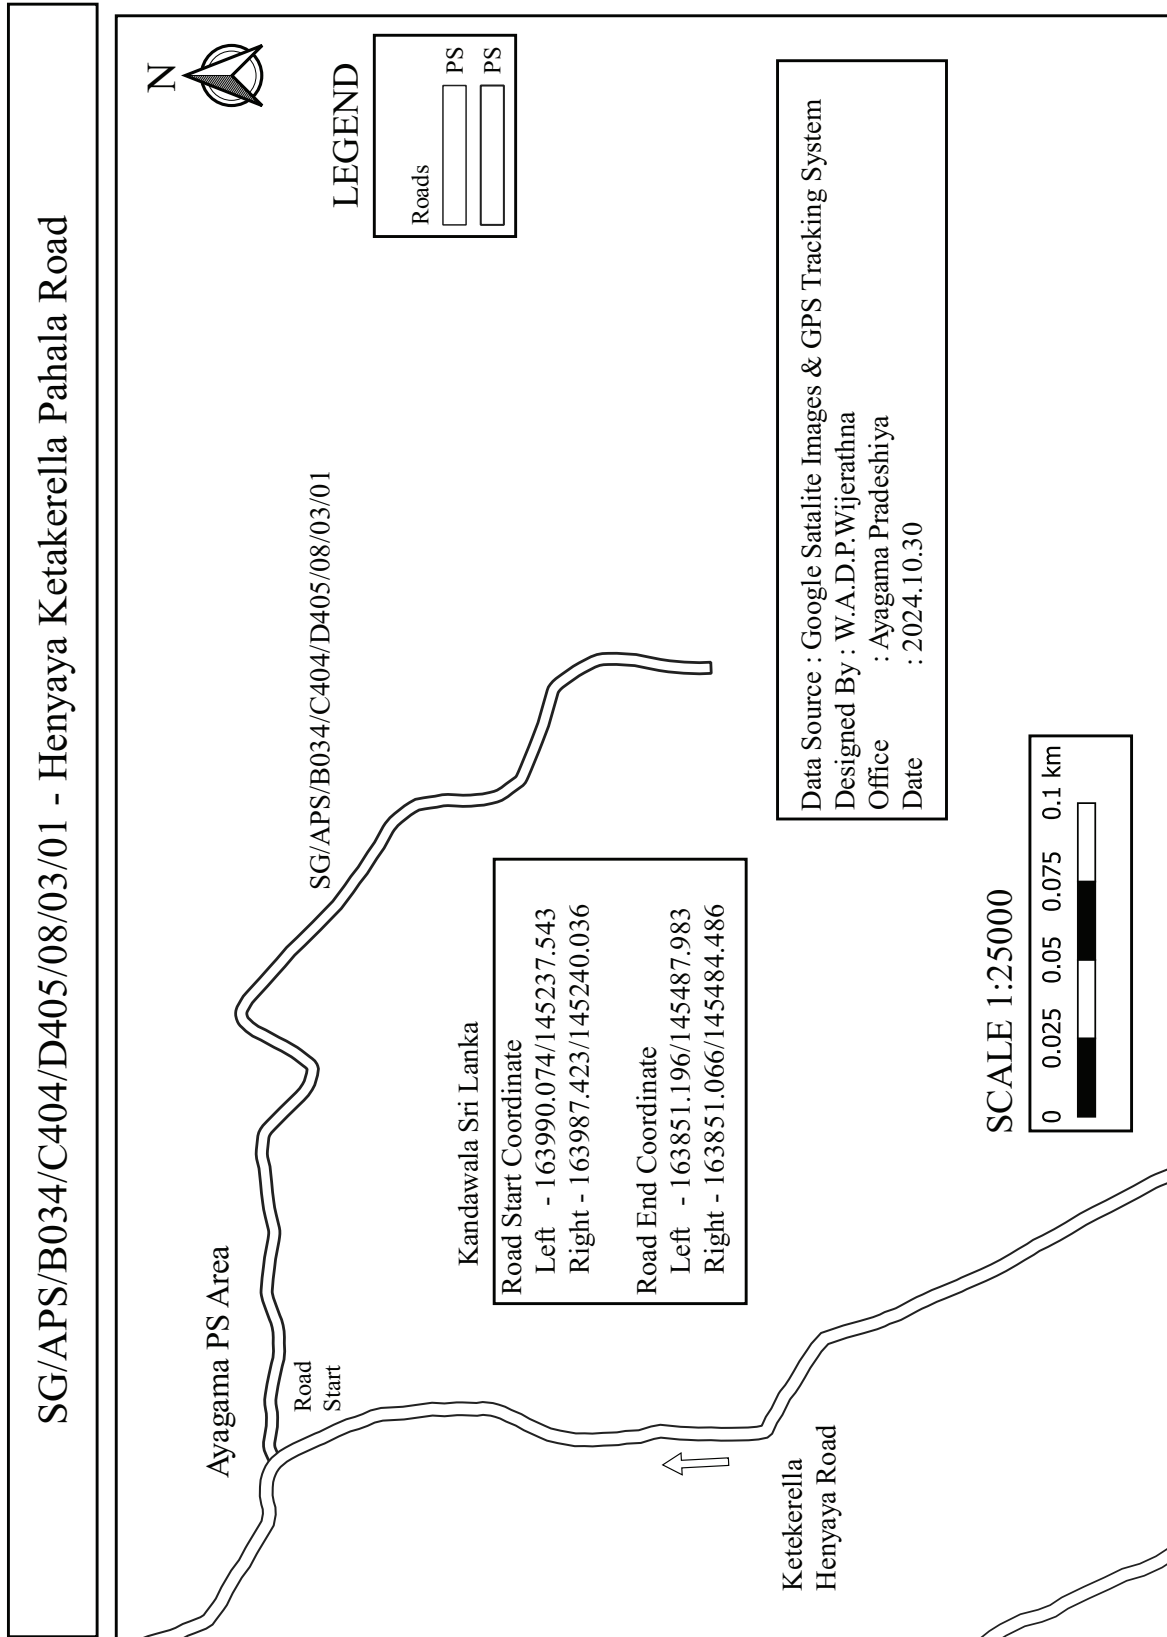

SG/APS/B034/C404/D405/09 - Akkara 36 First Lane

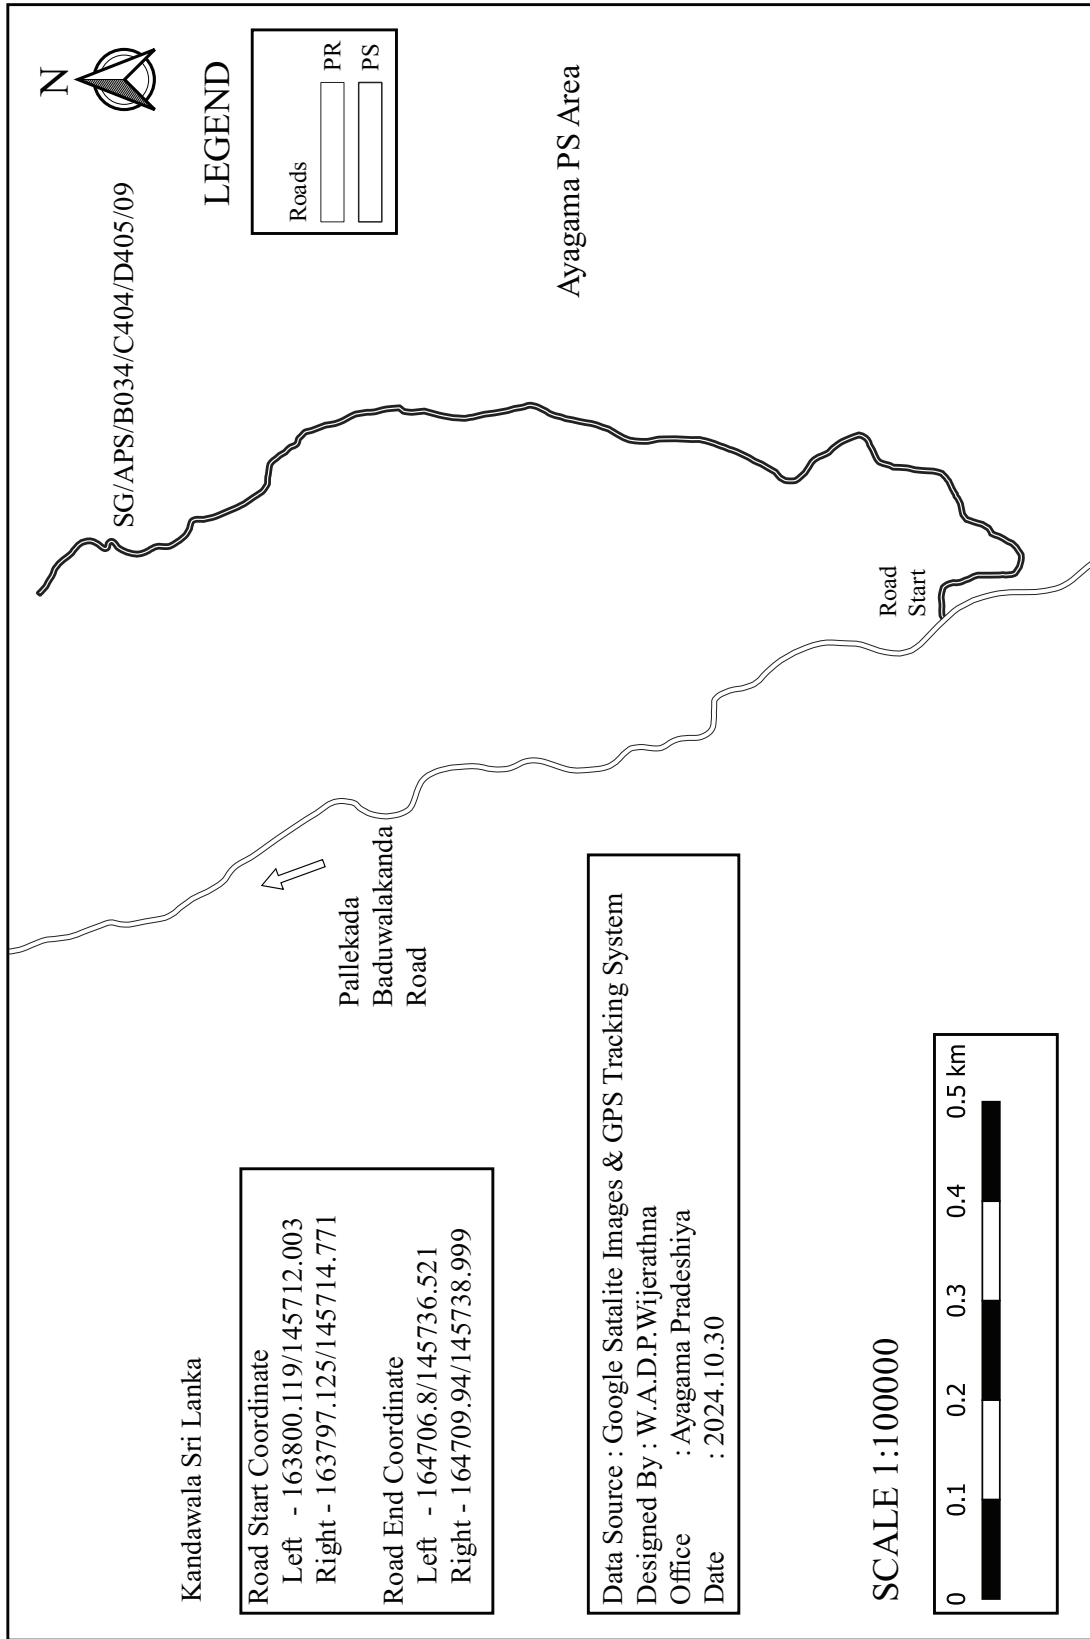

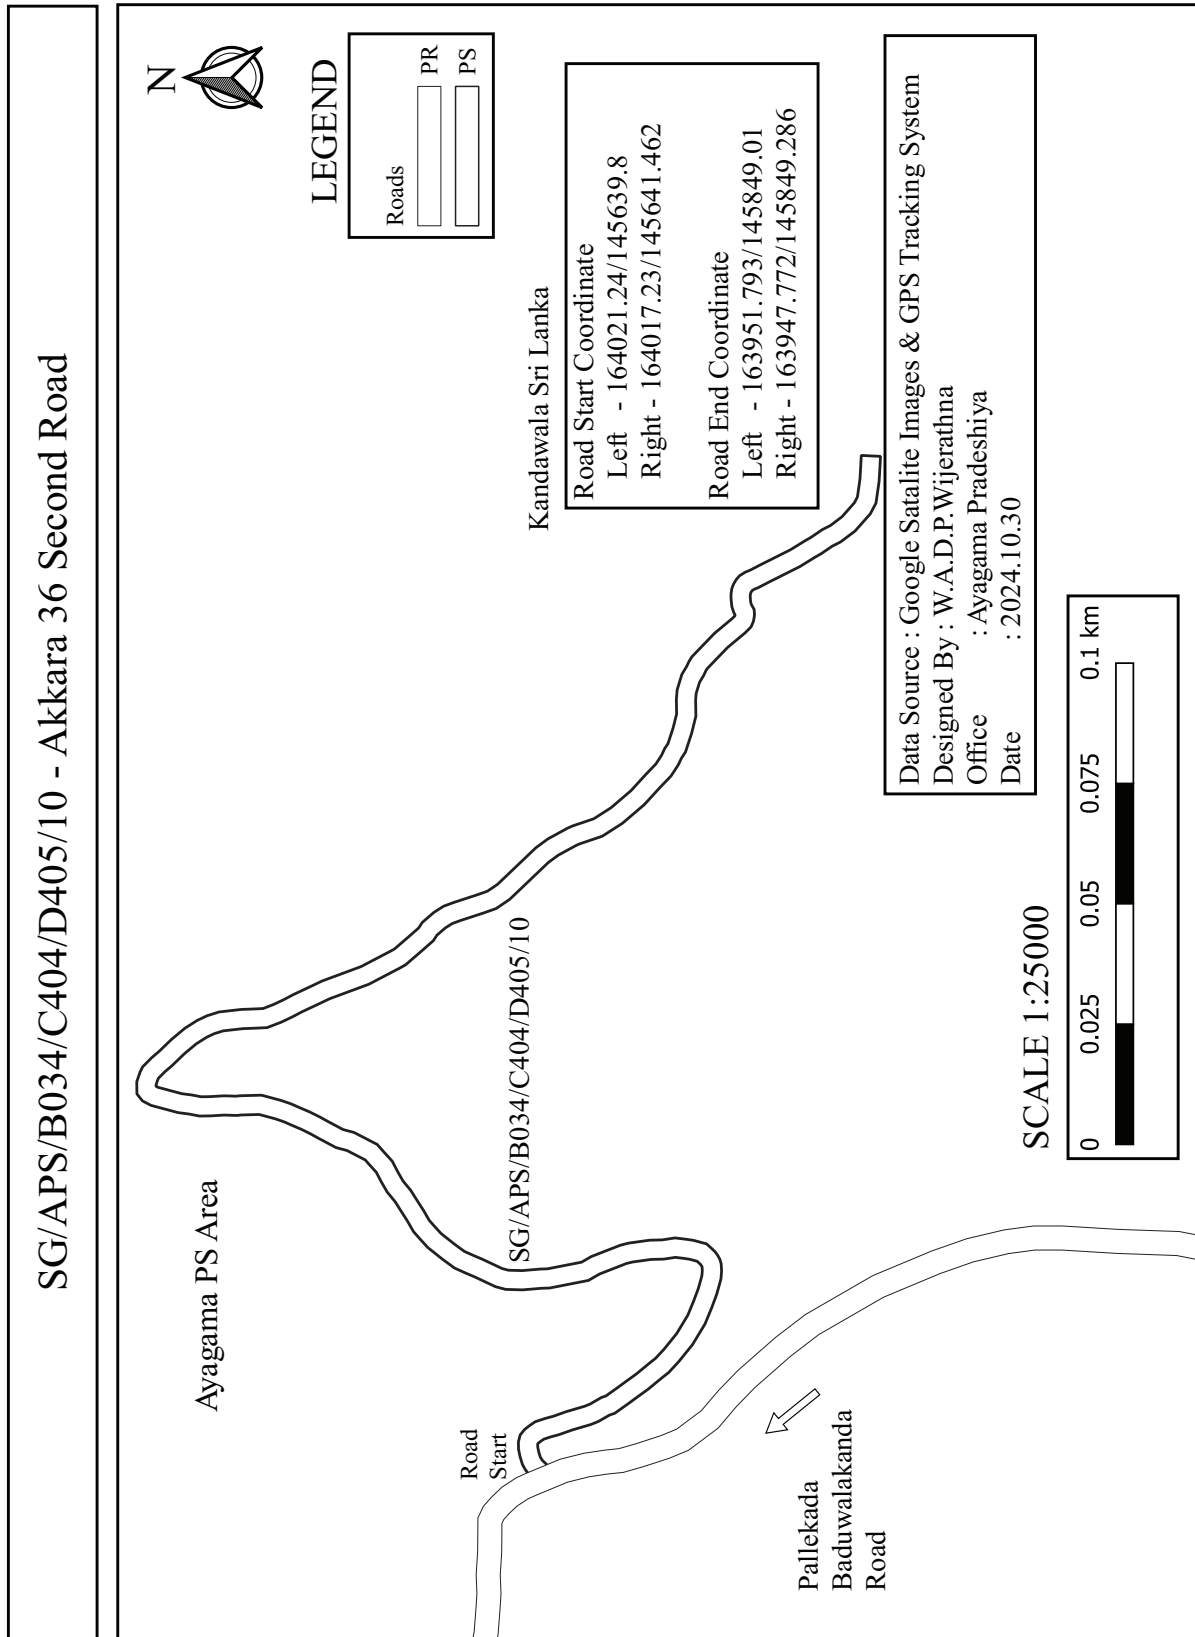

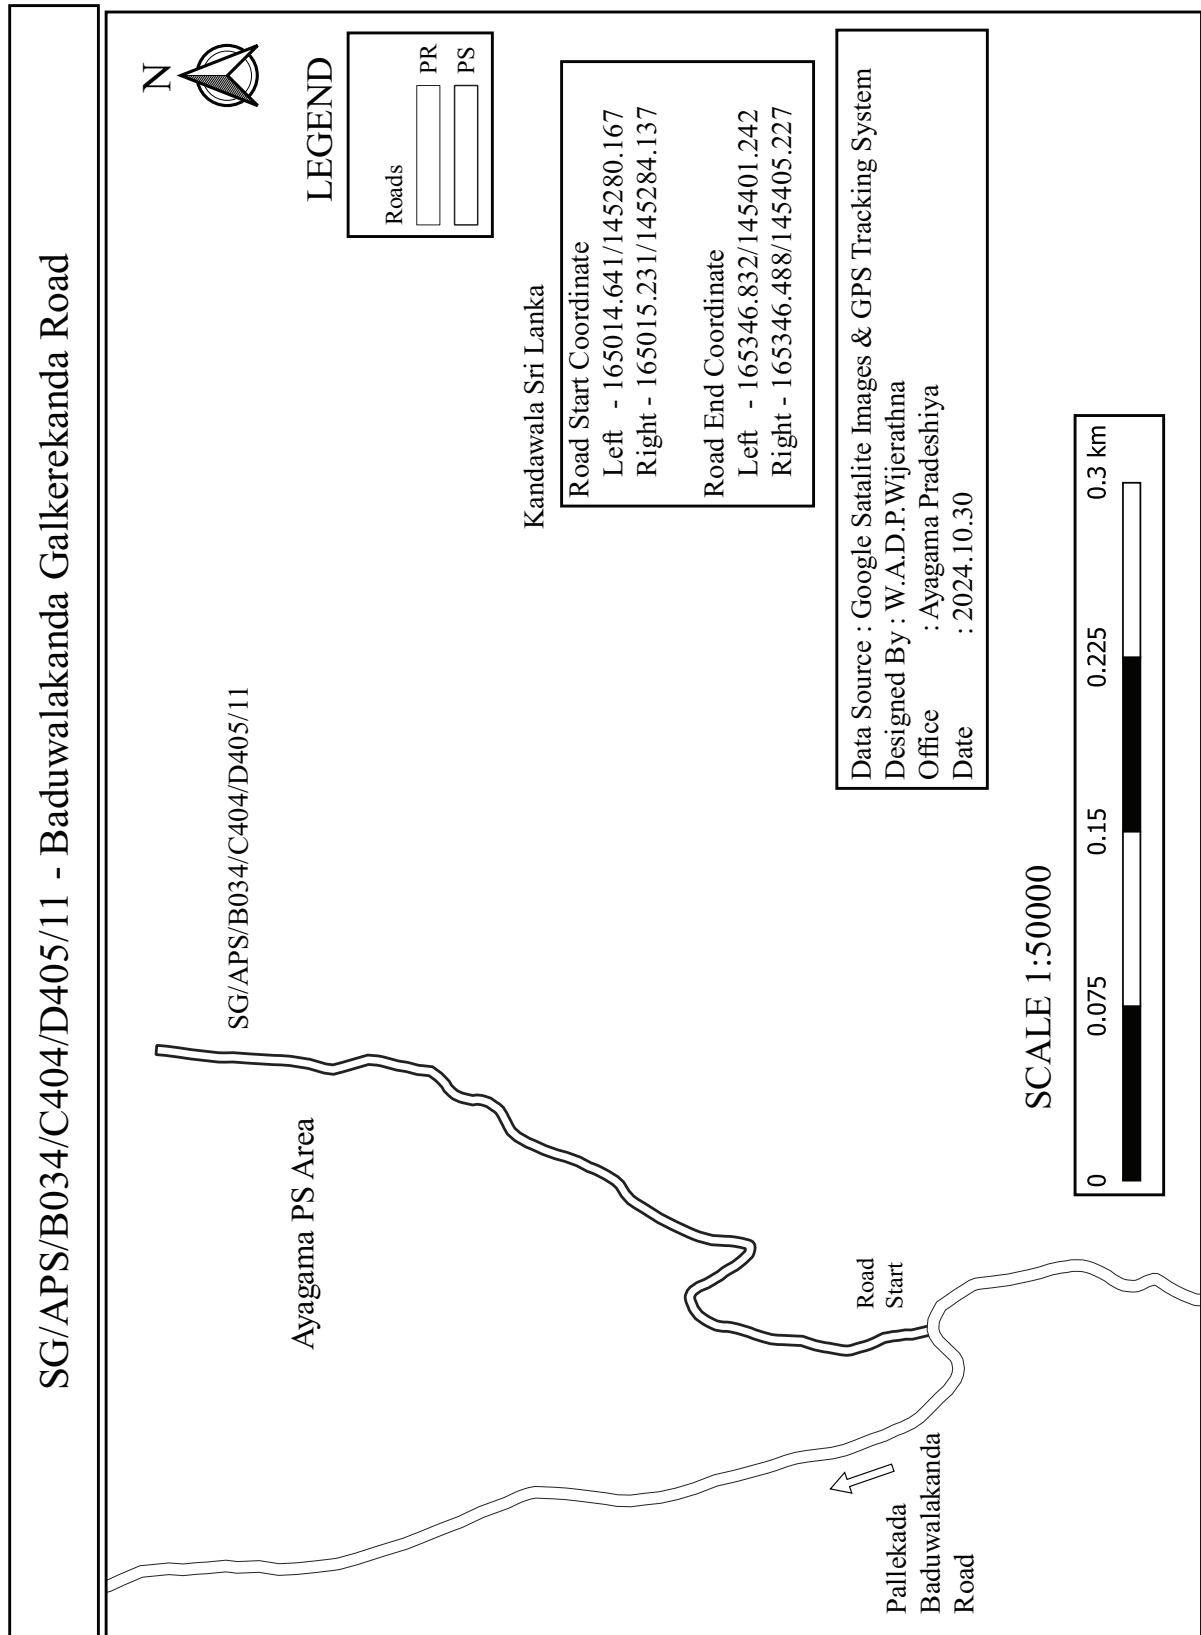

SG/APS/B034/C404/D405/11/01

Ayagama PS Area

N

LEGEND

Roads

PS

PS

Kandawala Sri Lanka

Road Start Coordinate

Left - 165158.3/145353.973

Right - 165152.821/145351.331

Road End Coordinate

Left - 166198.582/145939.273

Right - 166195.509/145937.524

Data Source : Google Satalite Images & GPS Tracking System

Designed By : W.A.D.P.Wijerathna

Office : Ayagama Pradeshiya

Date : 2024.10.30

SCALE 1:100000


0 0.1 0.2 0.3 0.4 0.5 km


Baduwalakanda


Galkerekanda


Road


Road Start

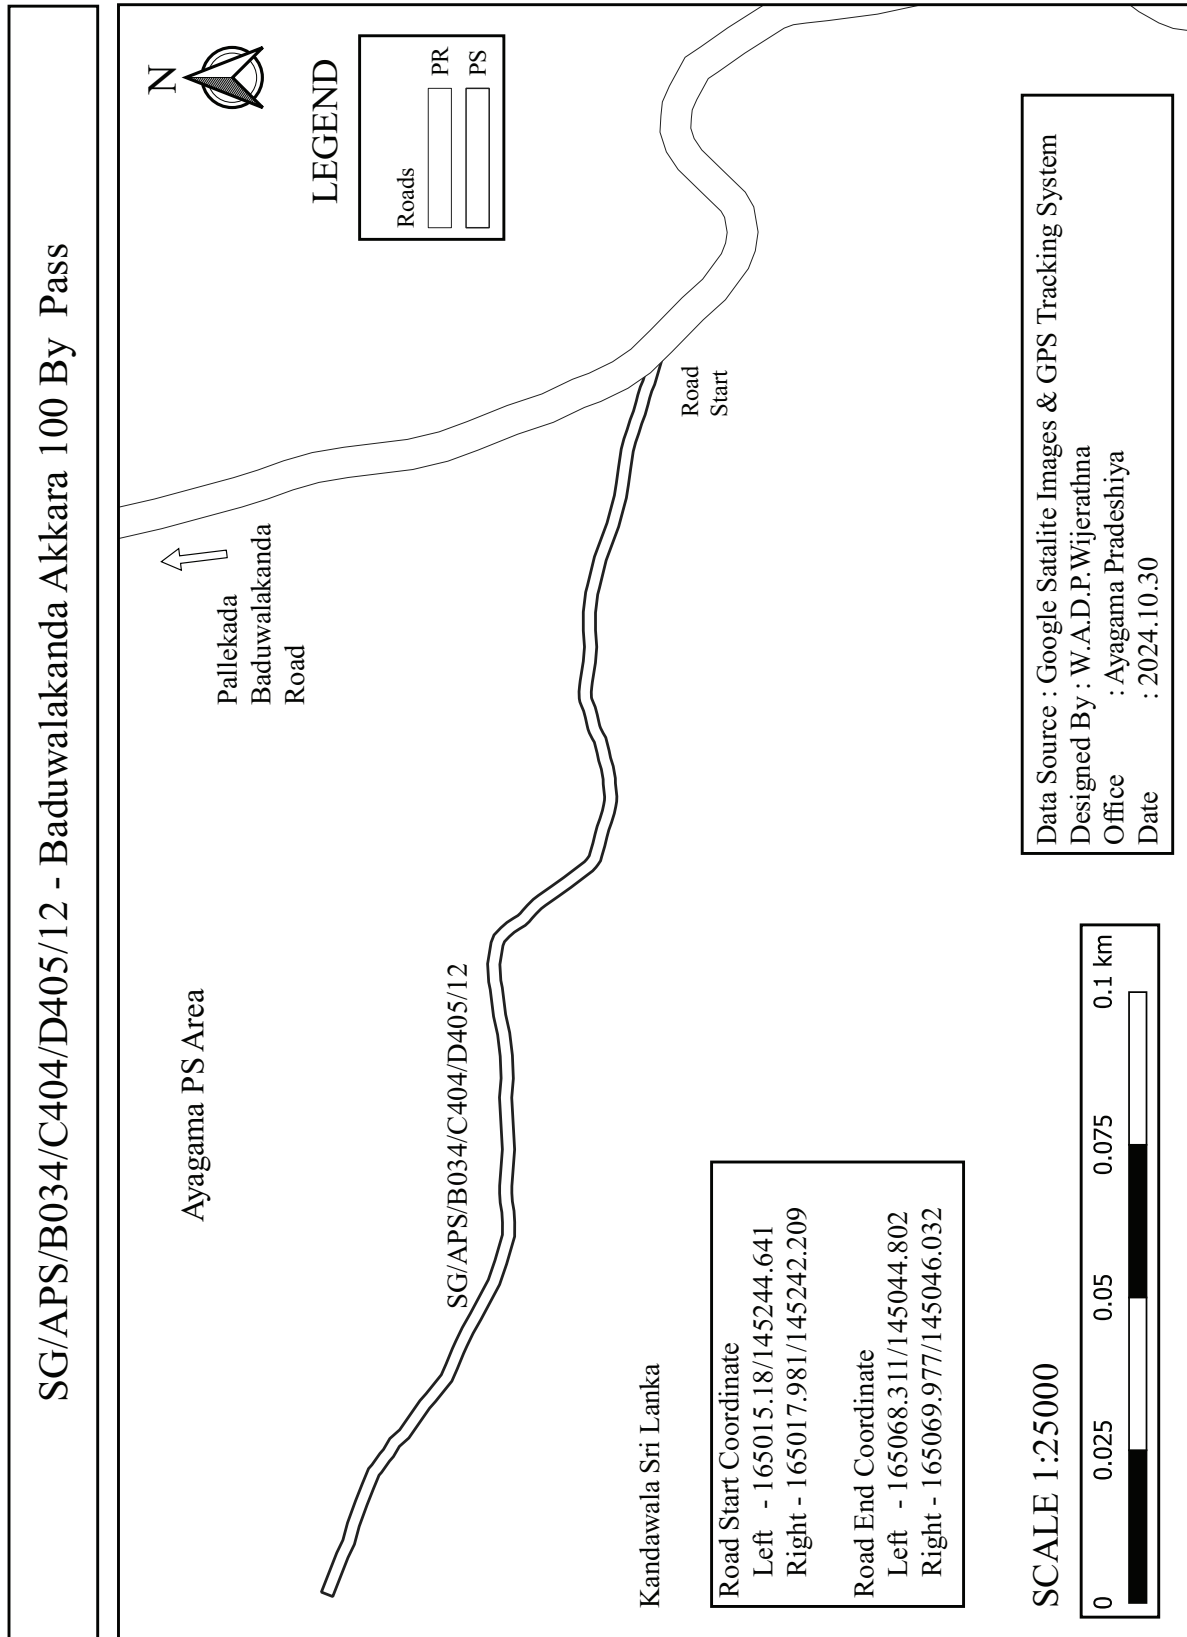


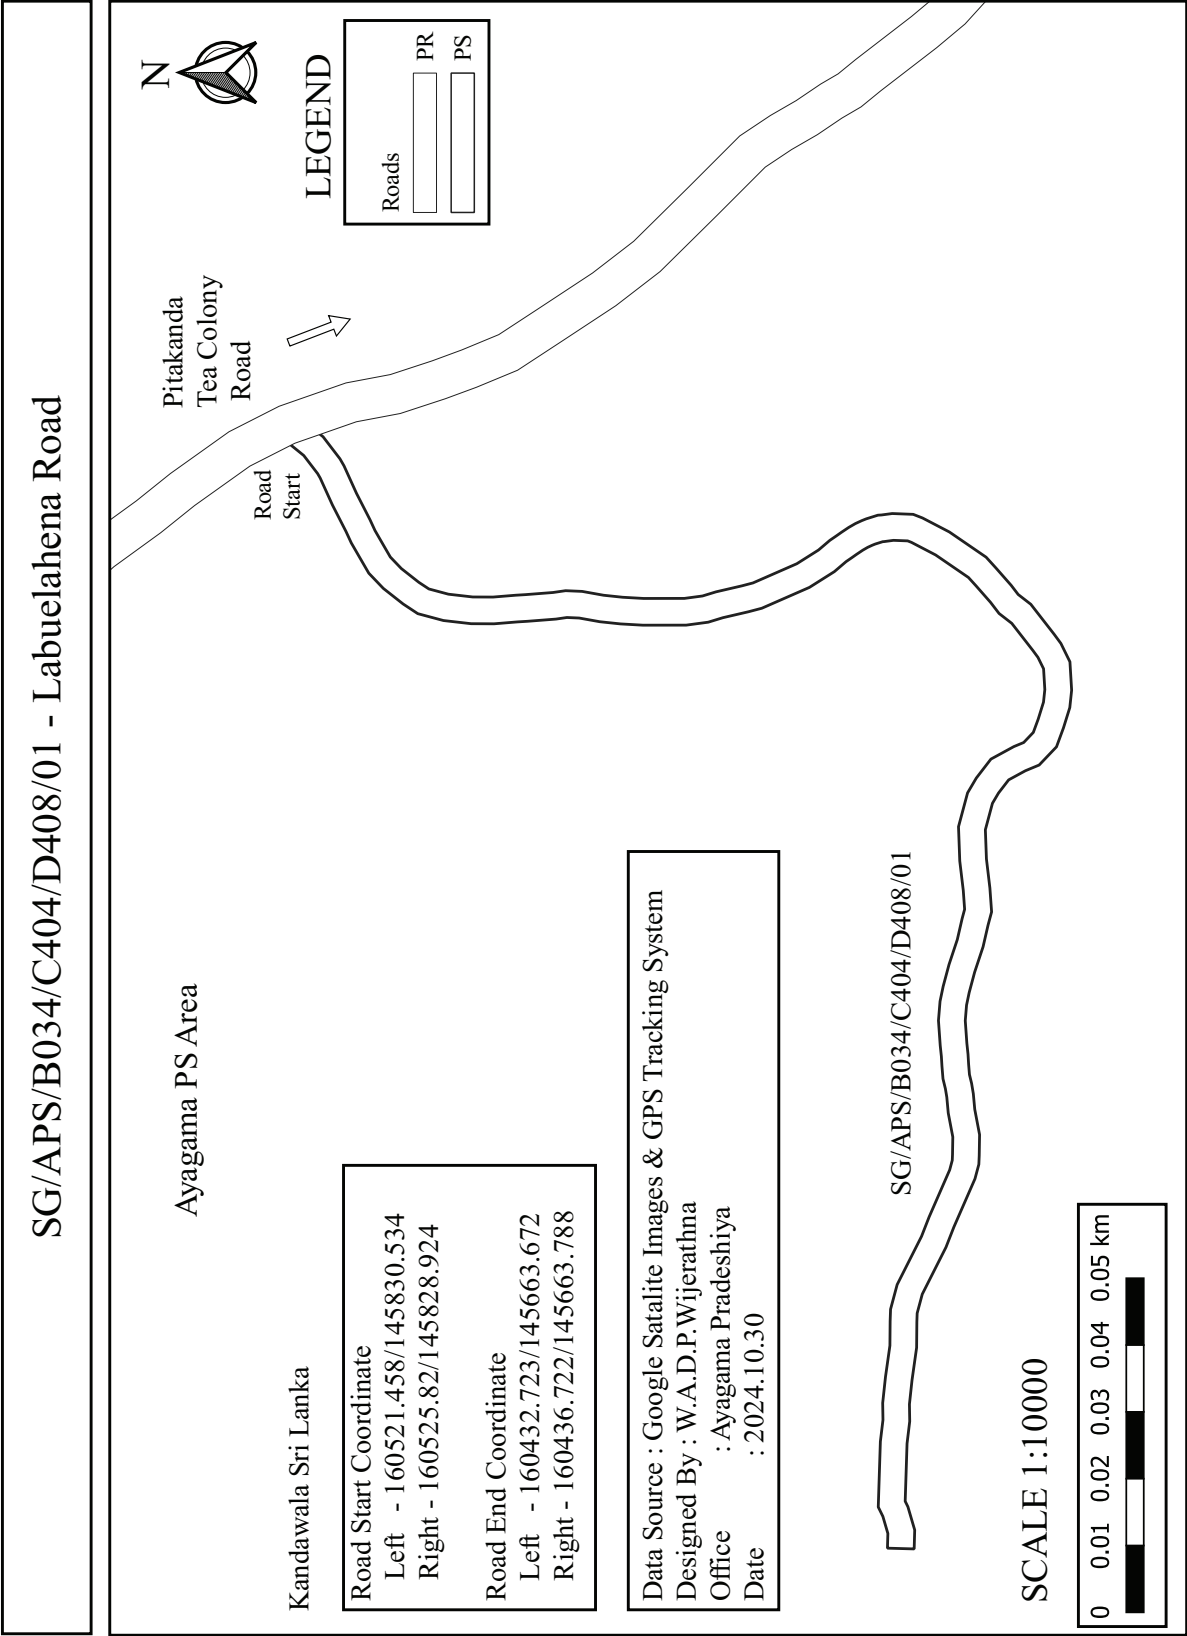


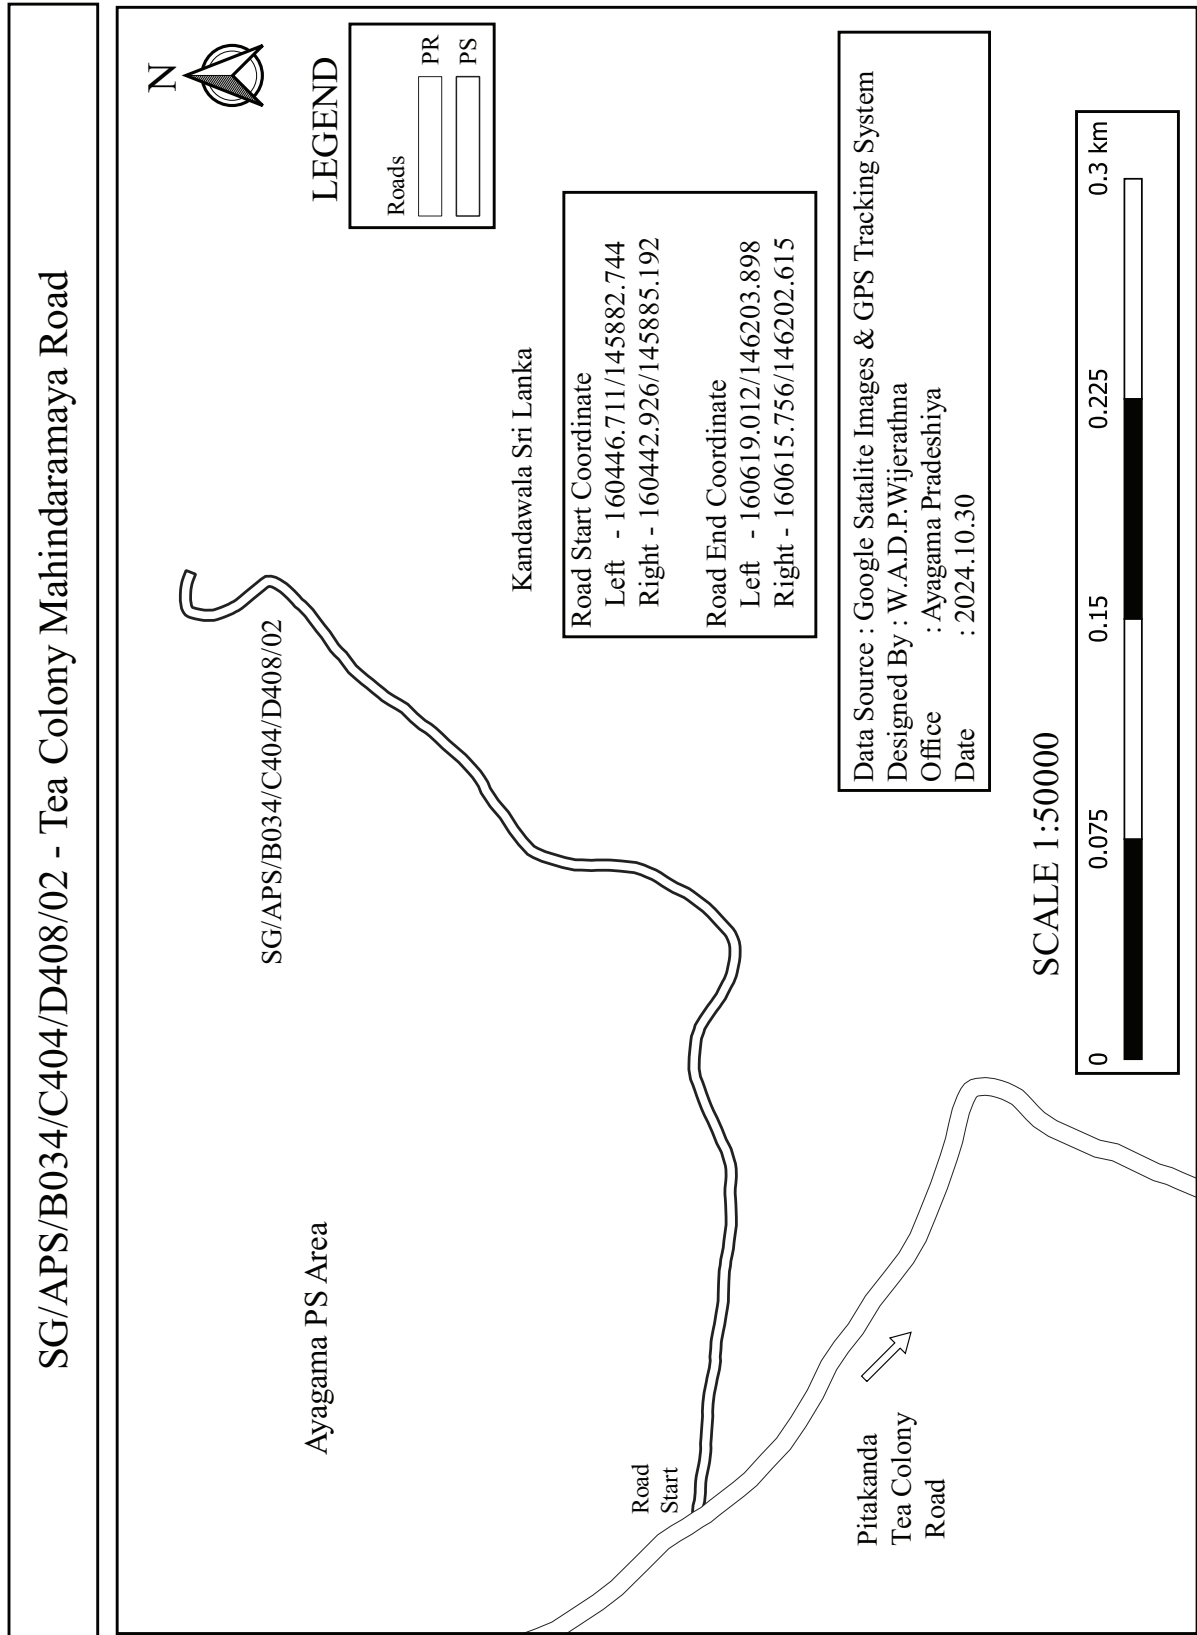


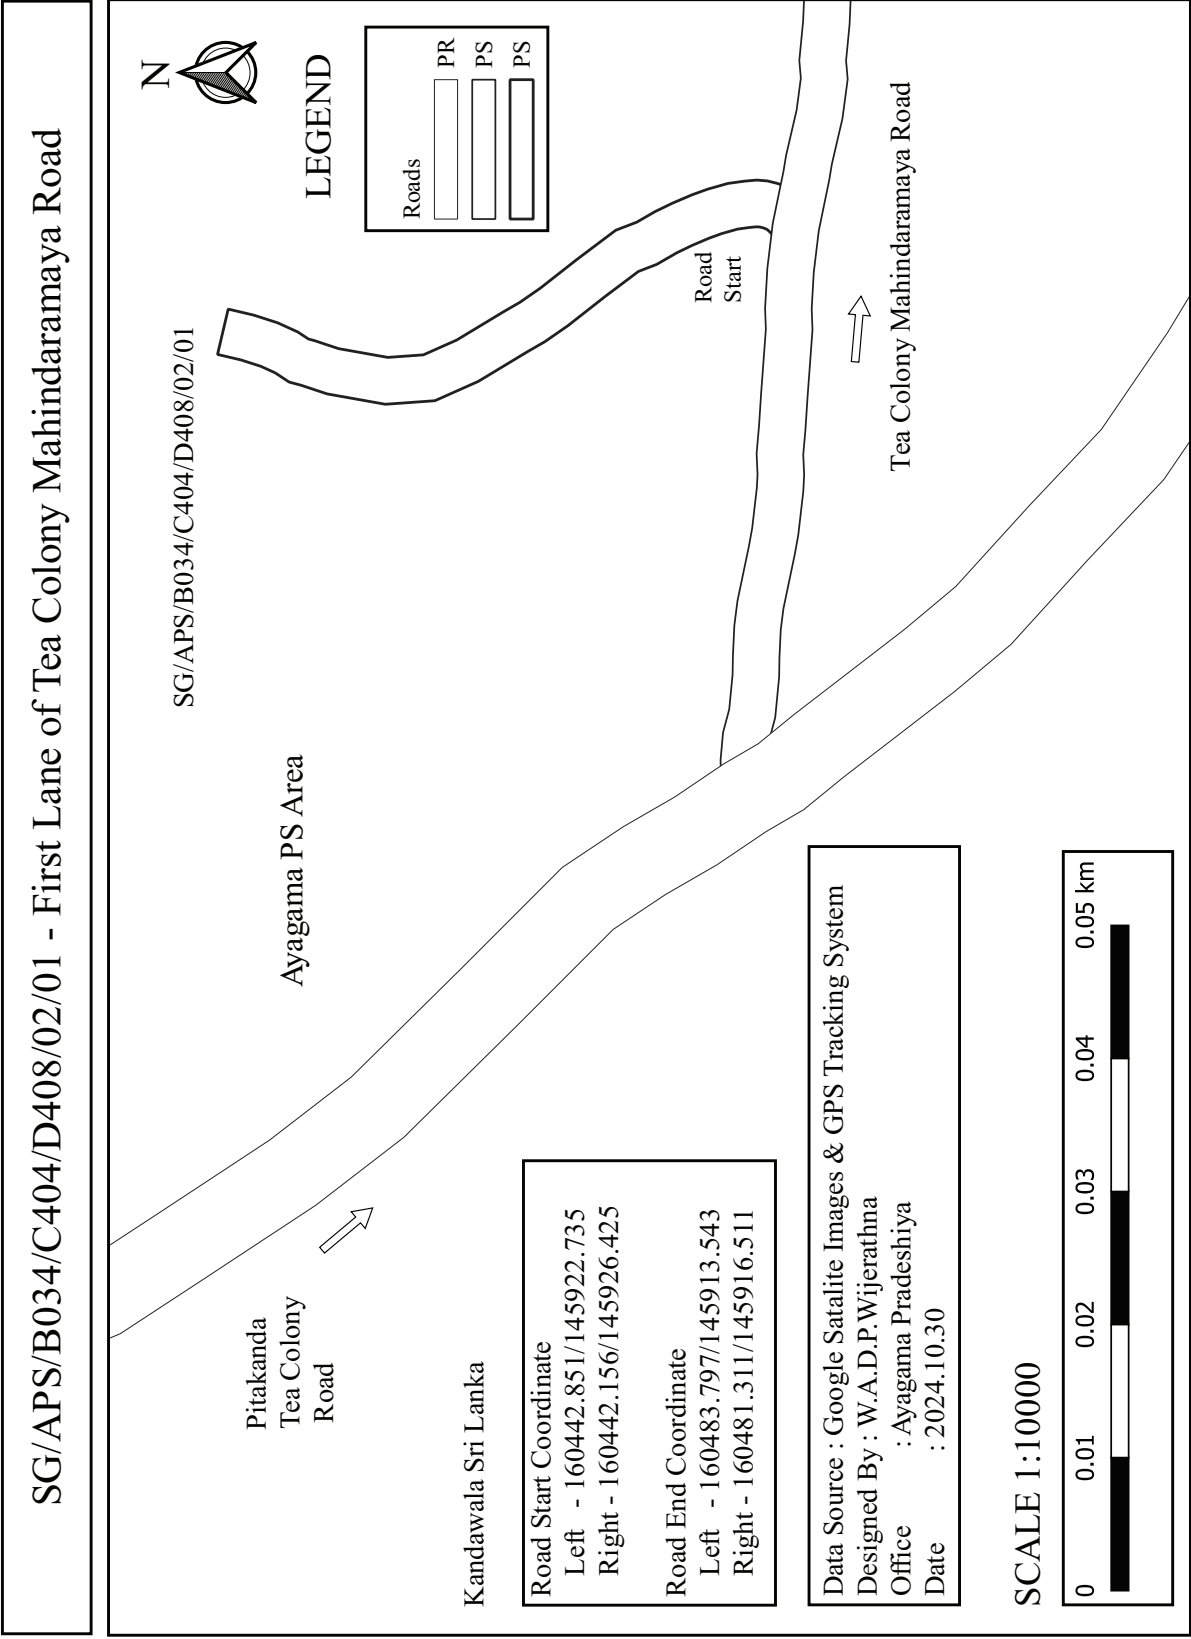

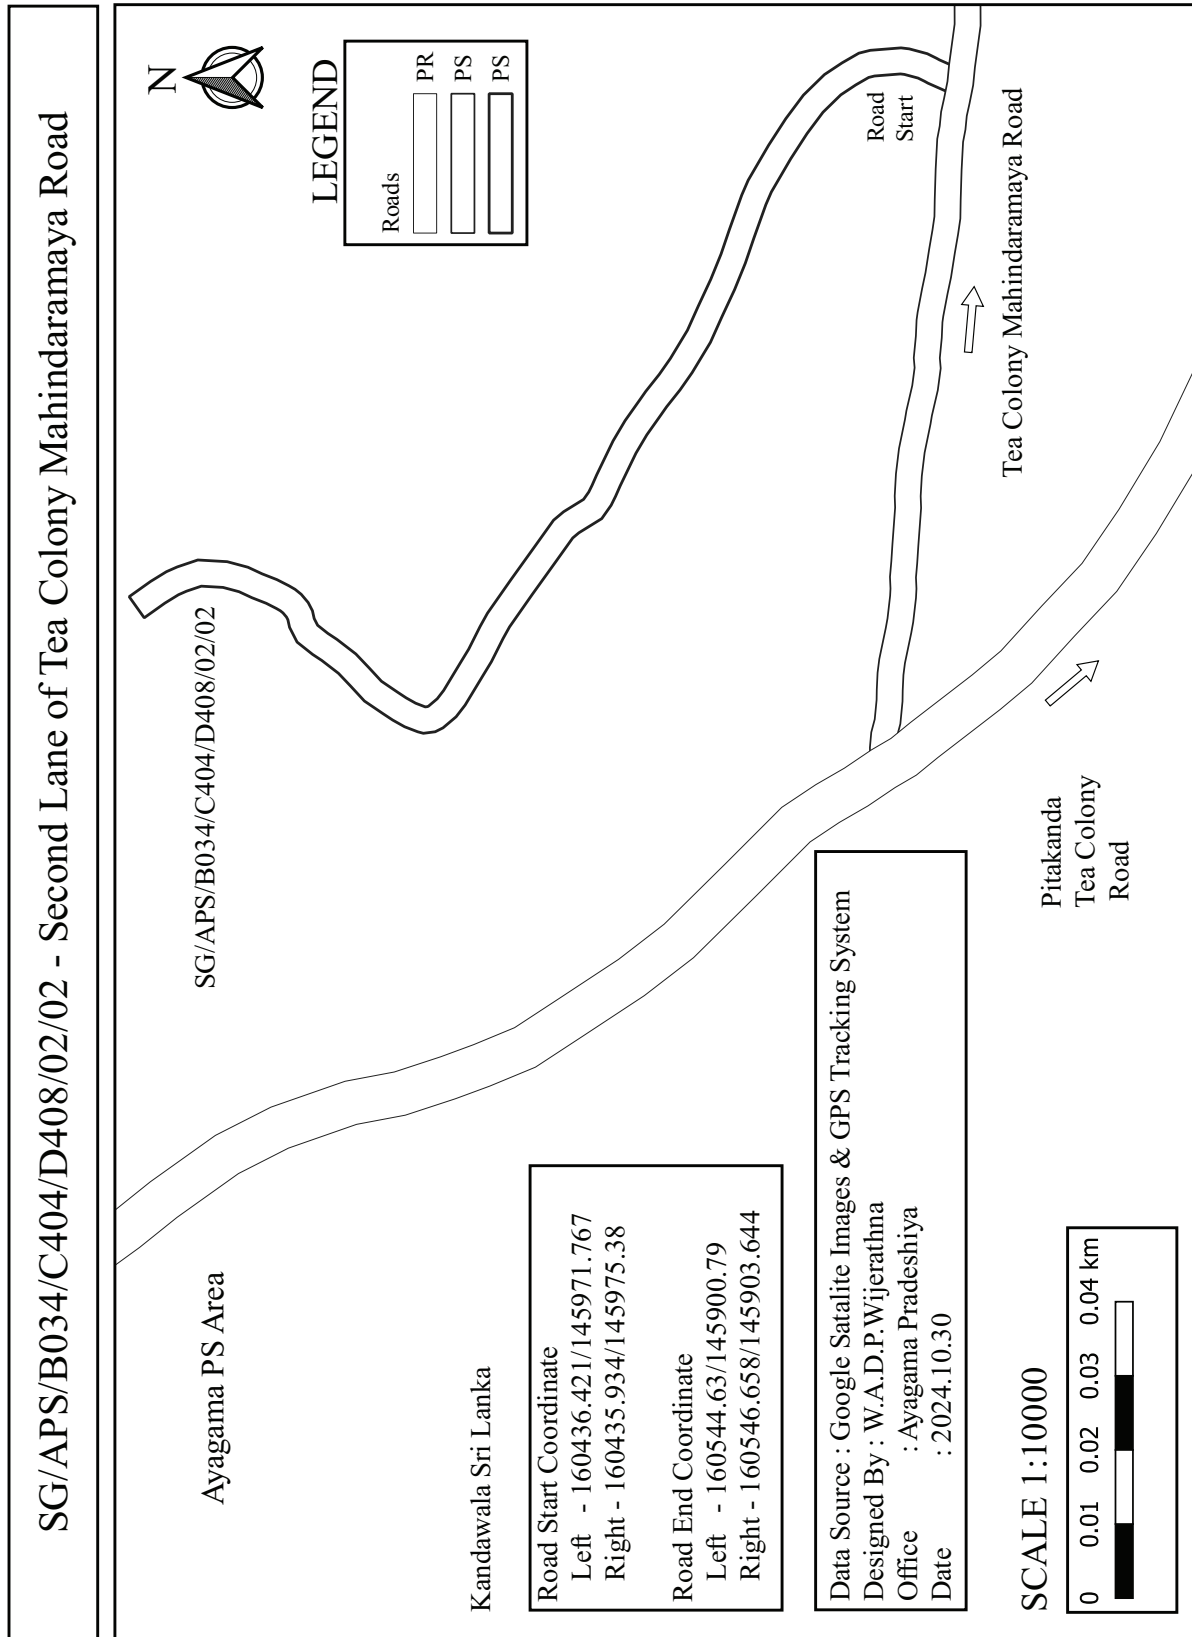


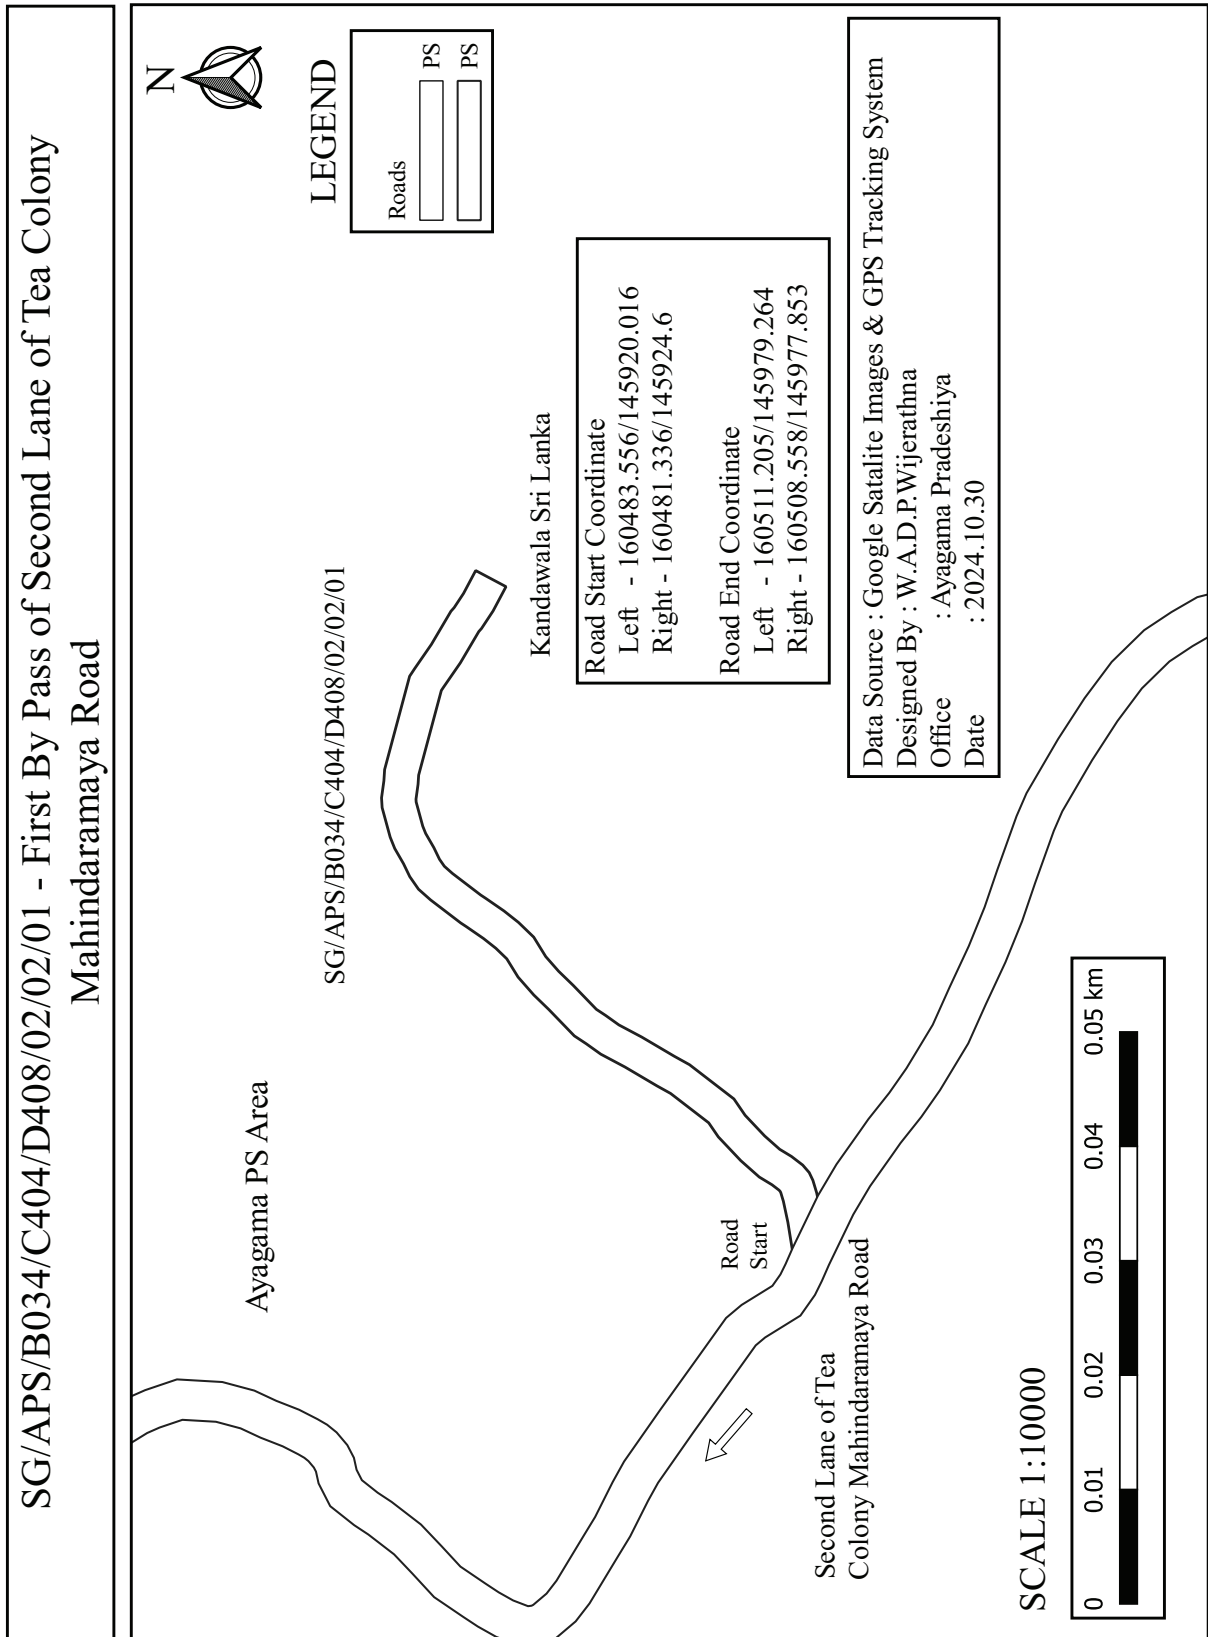


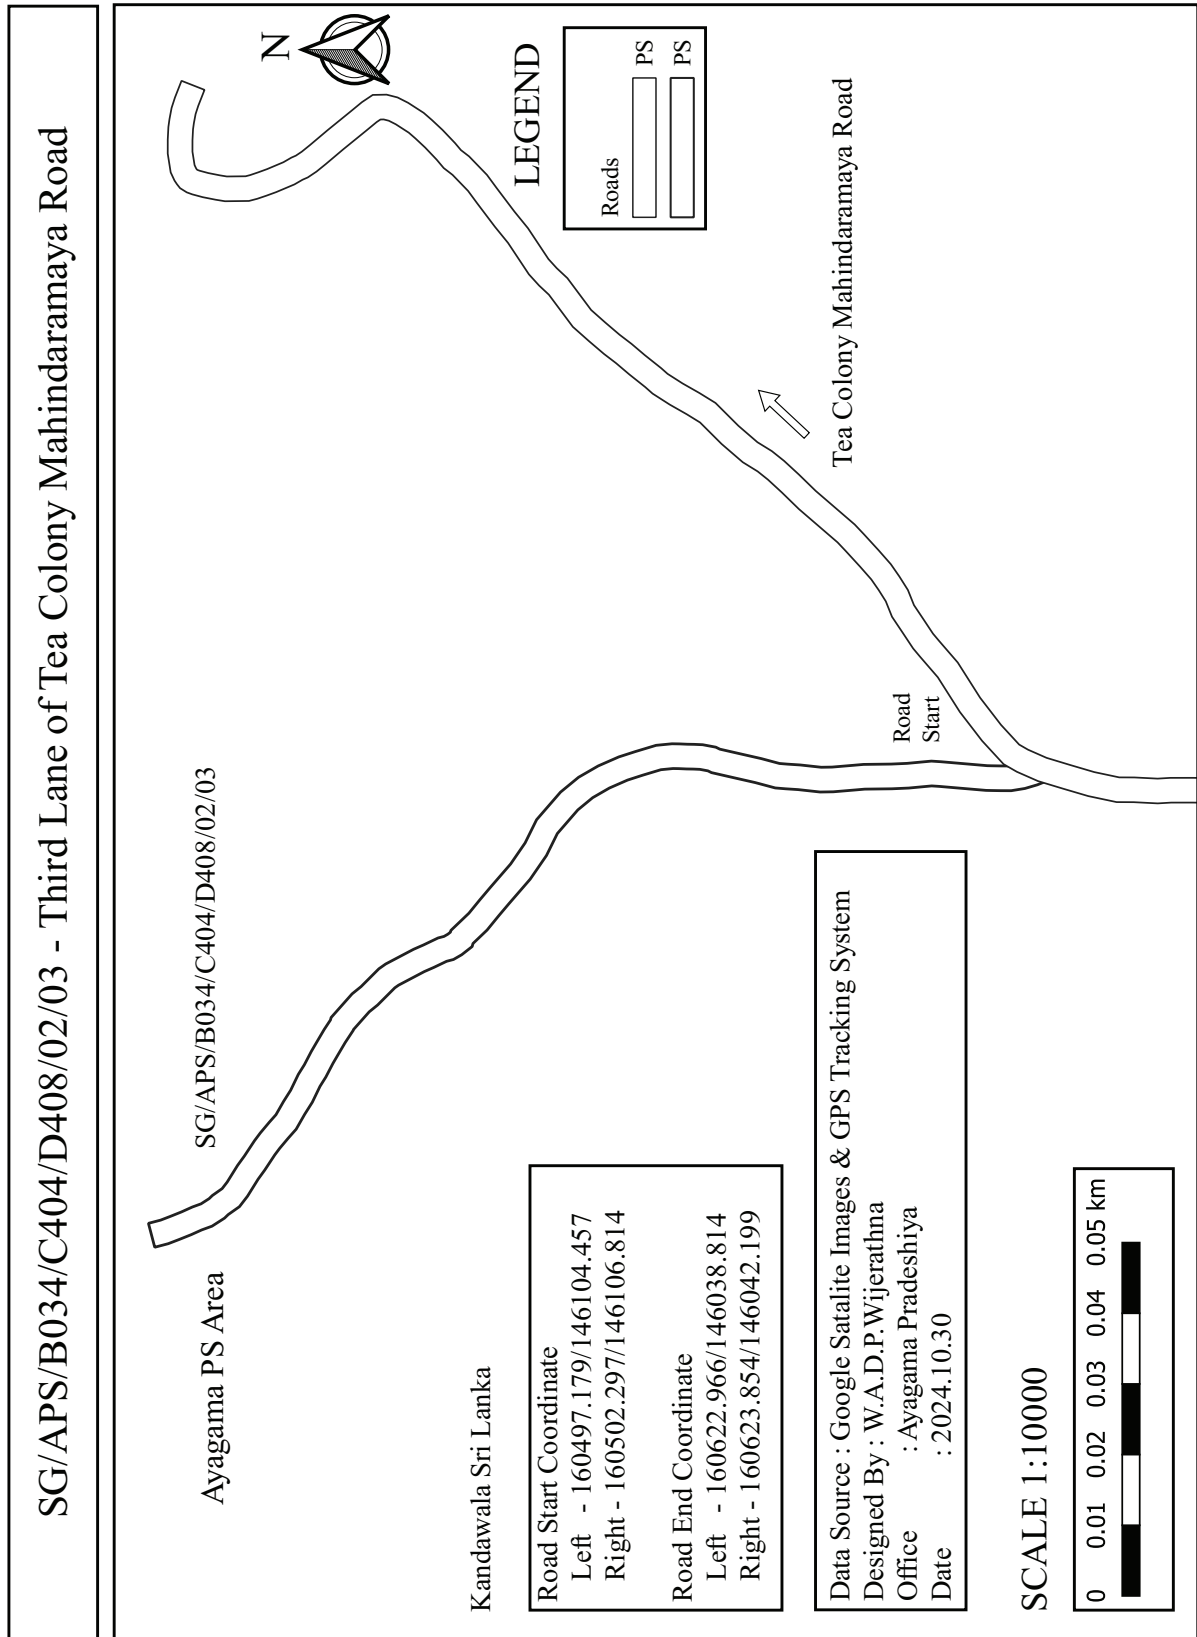


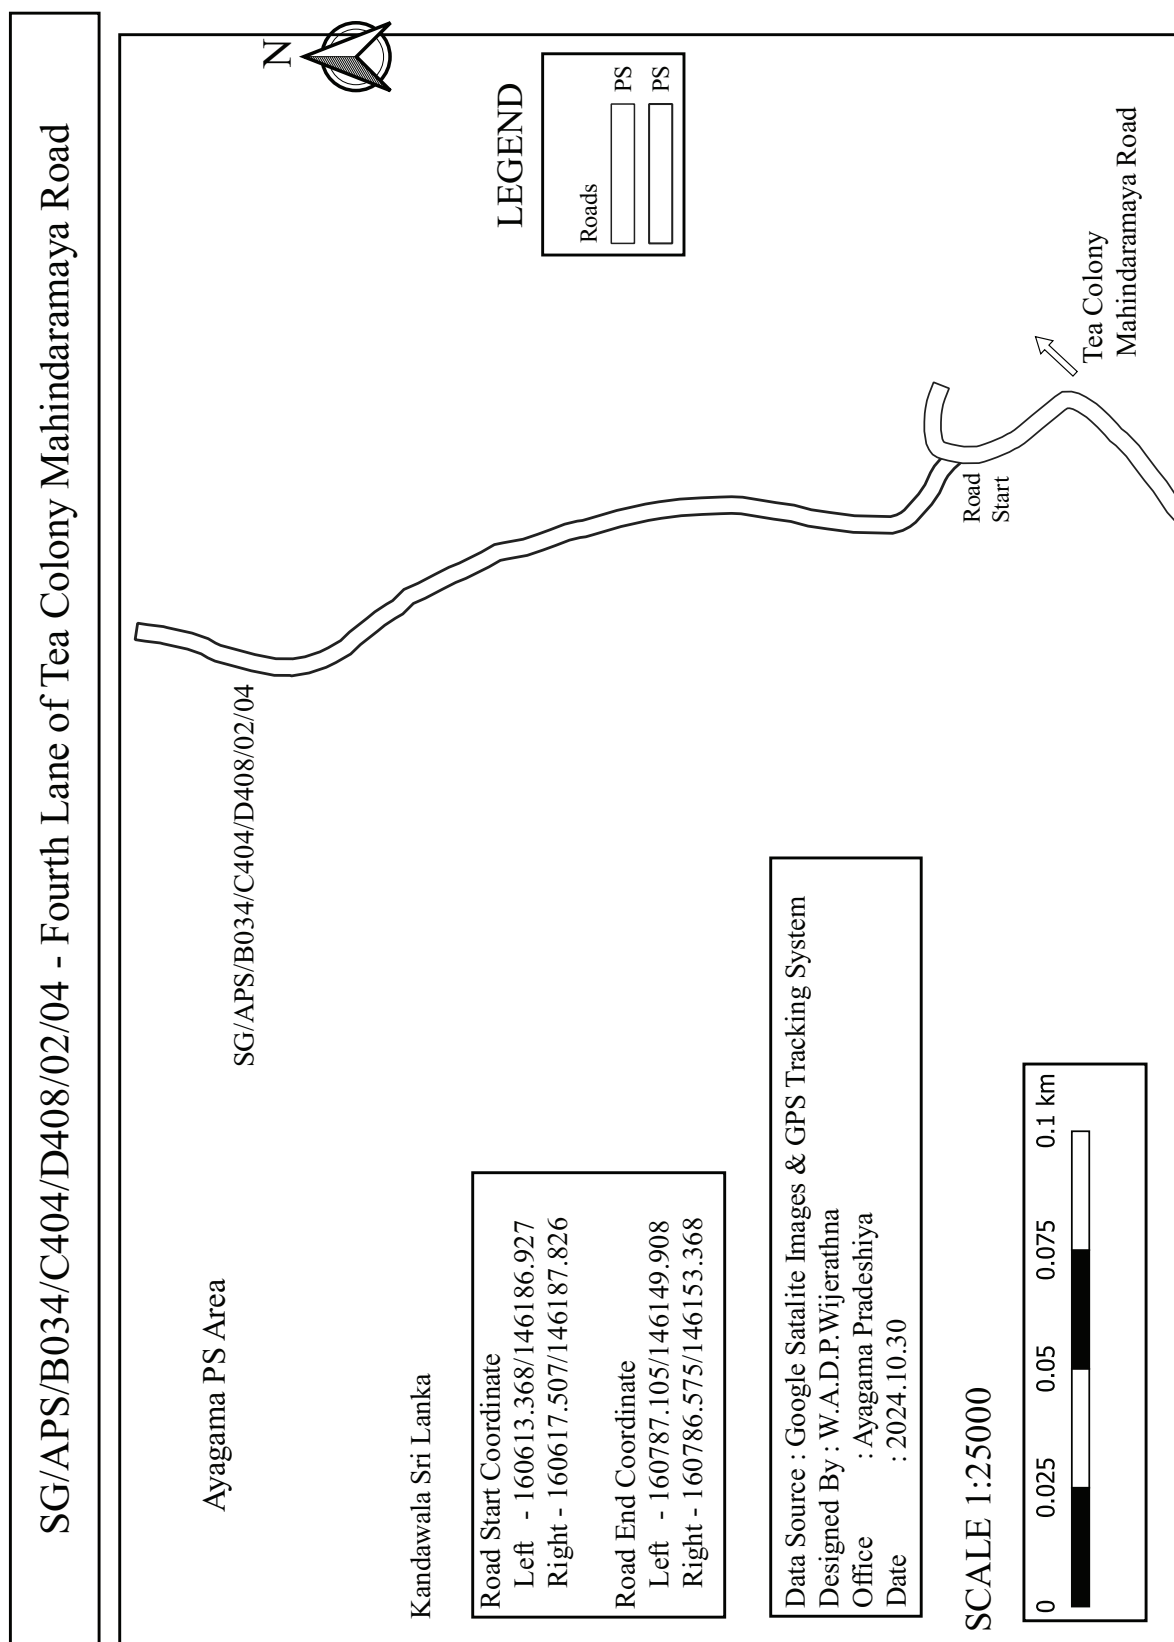


SG/APS/B034/C404/D408/03 - Mahindaramaya First Lane

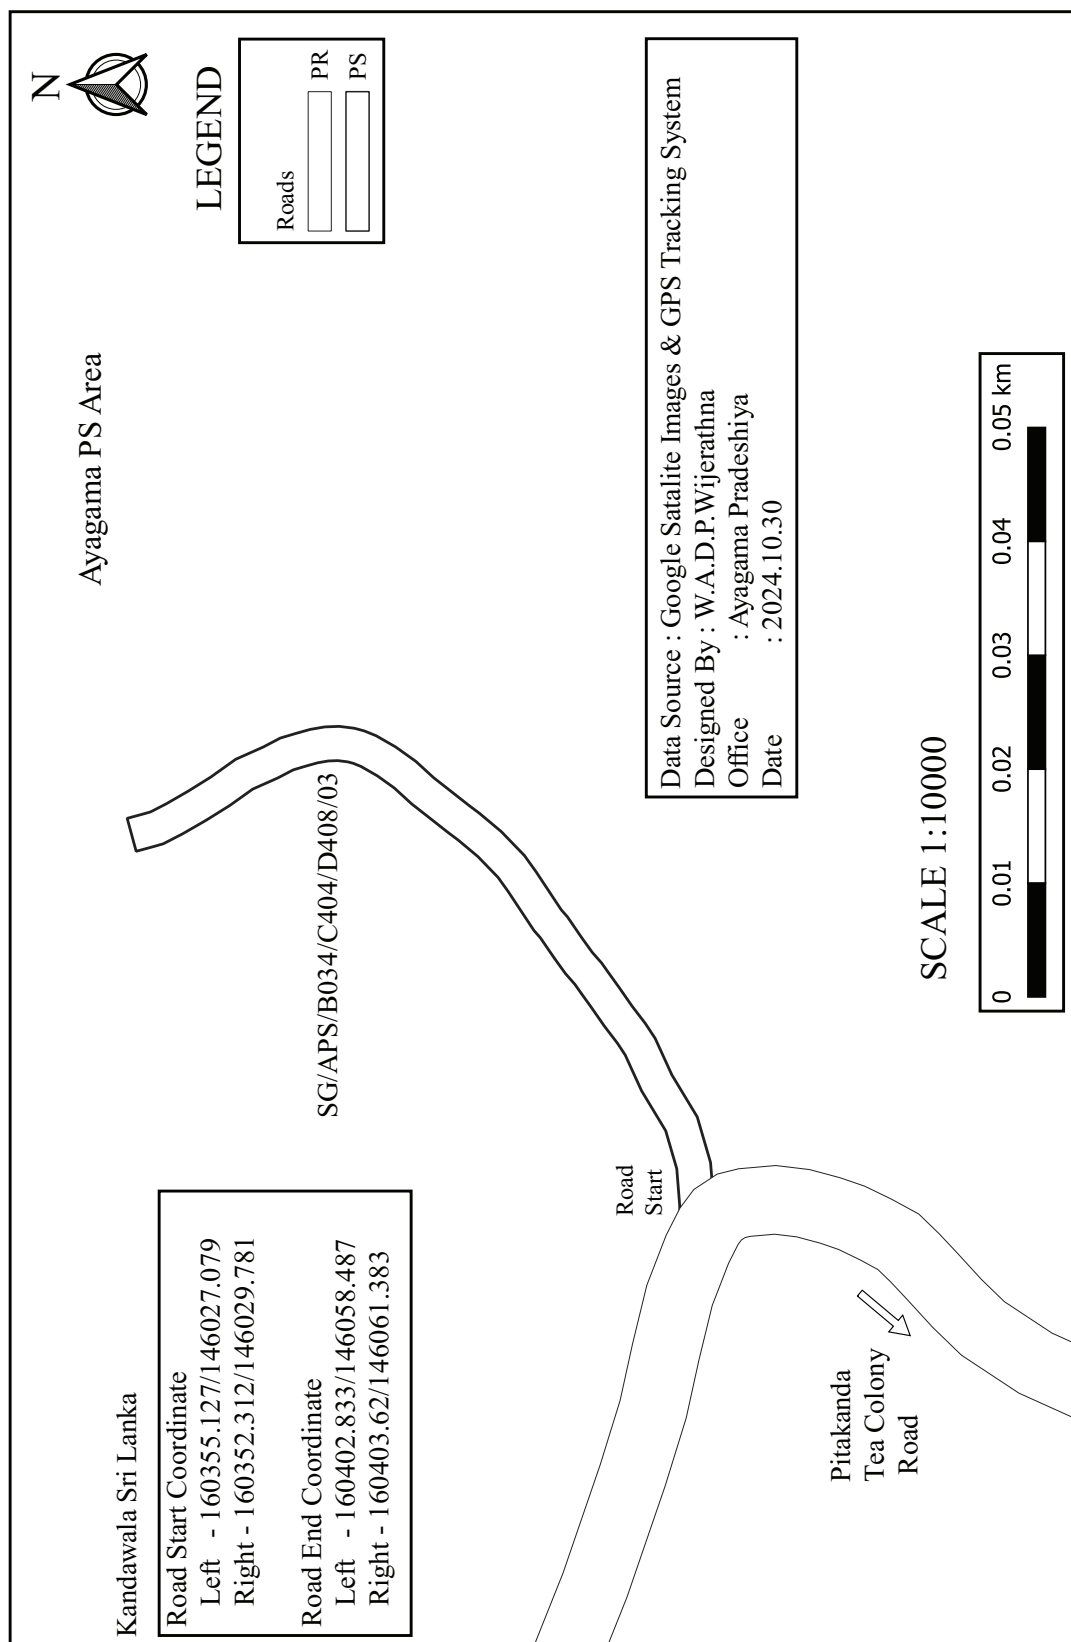


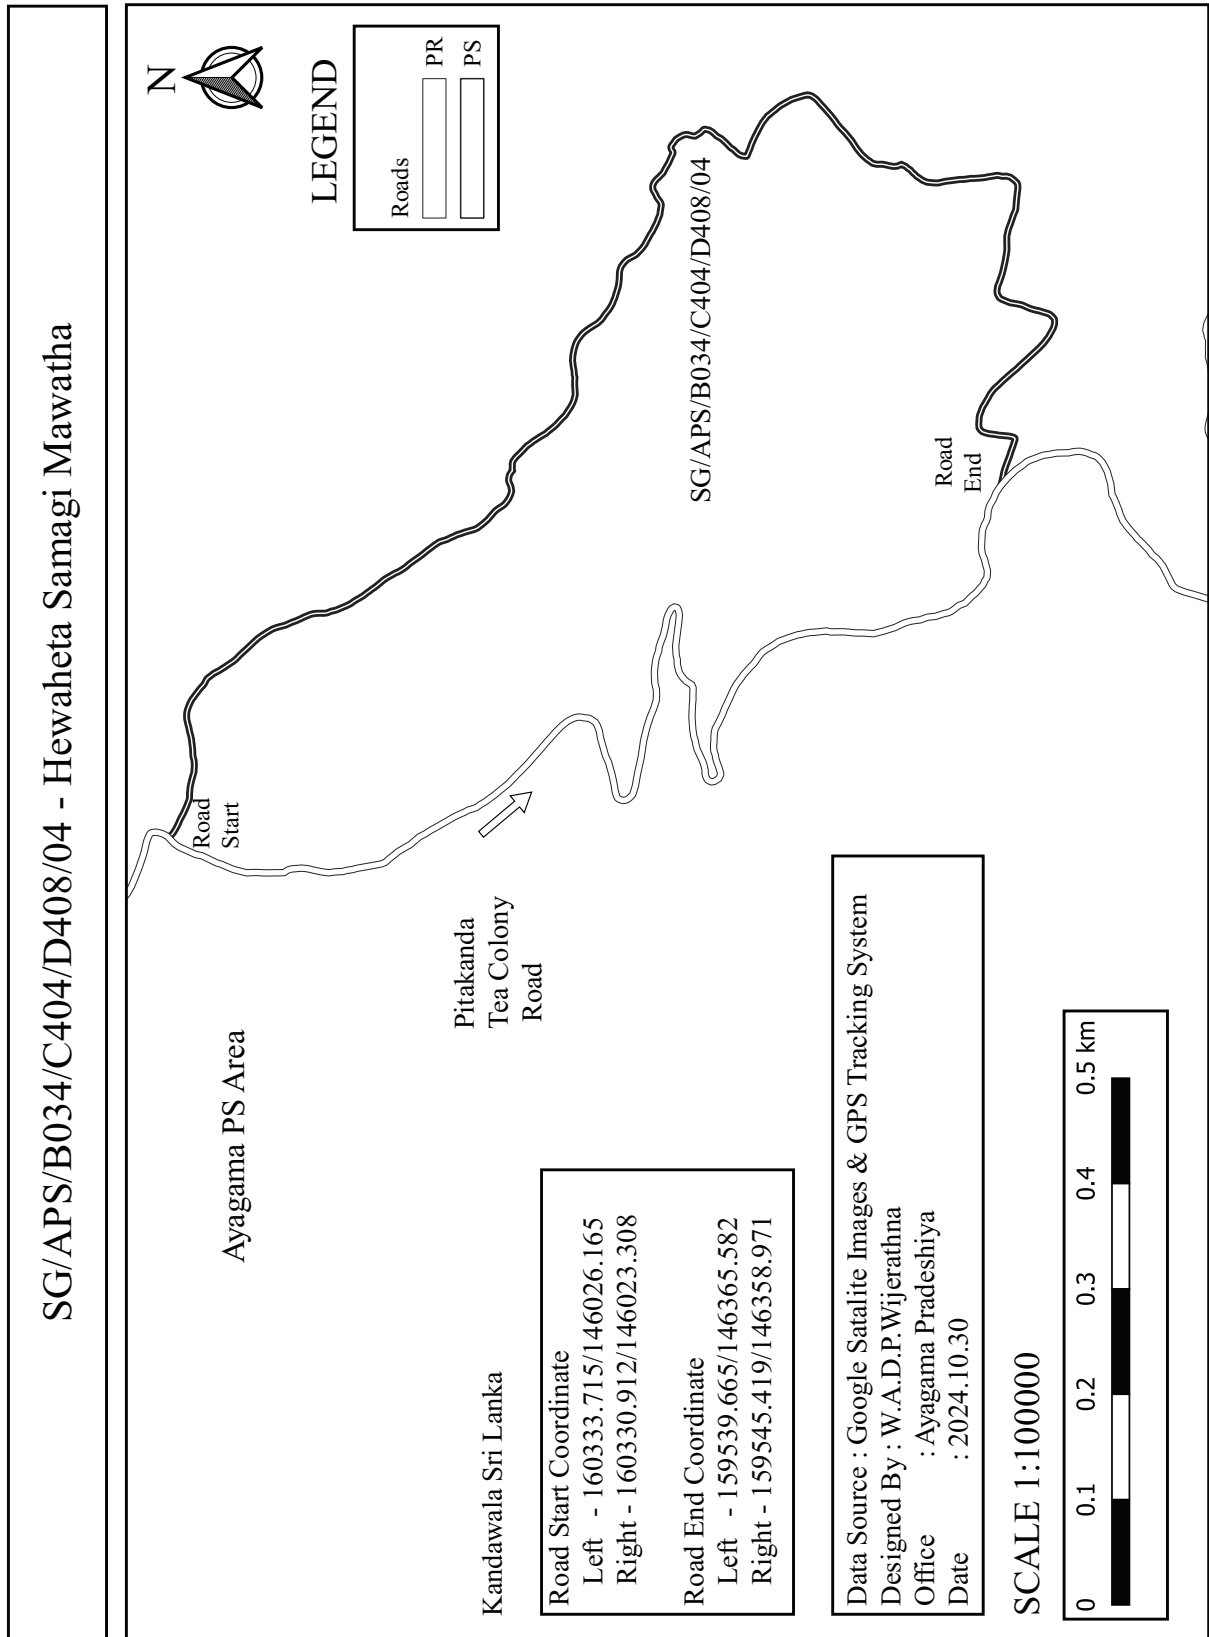


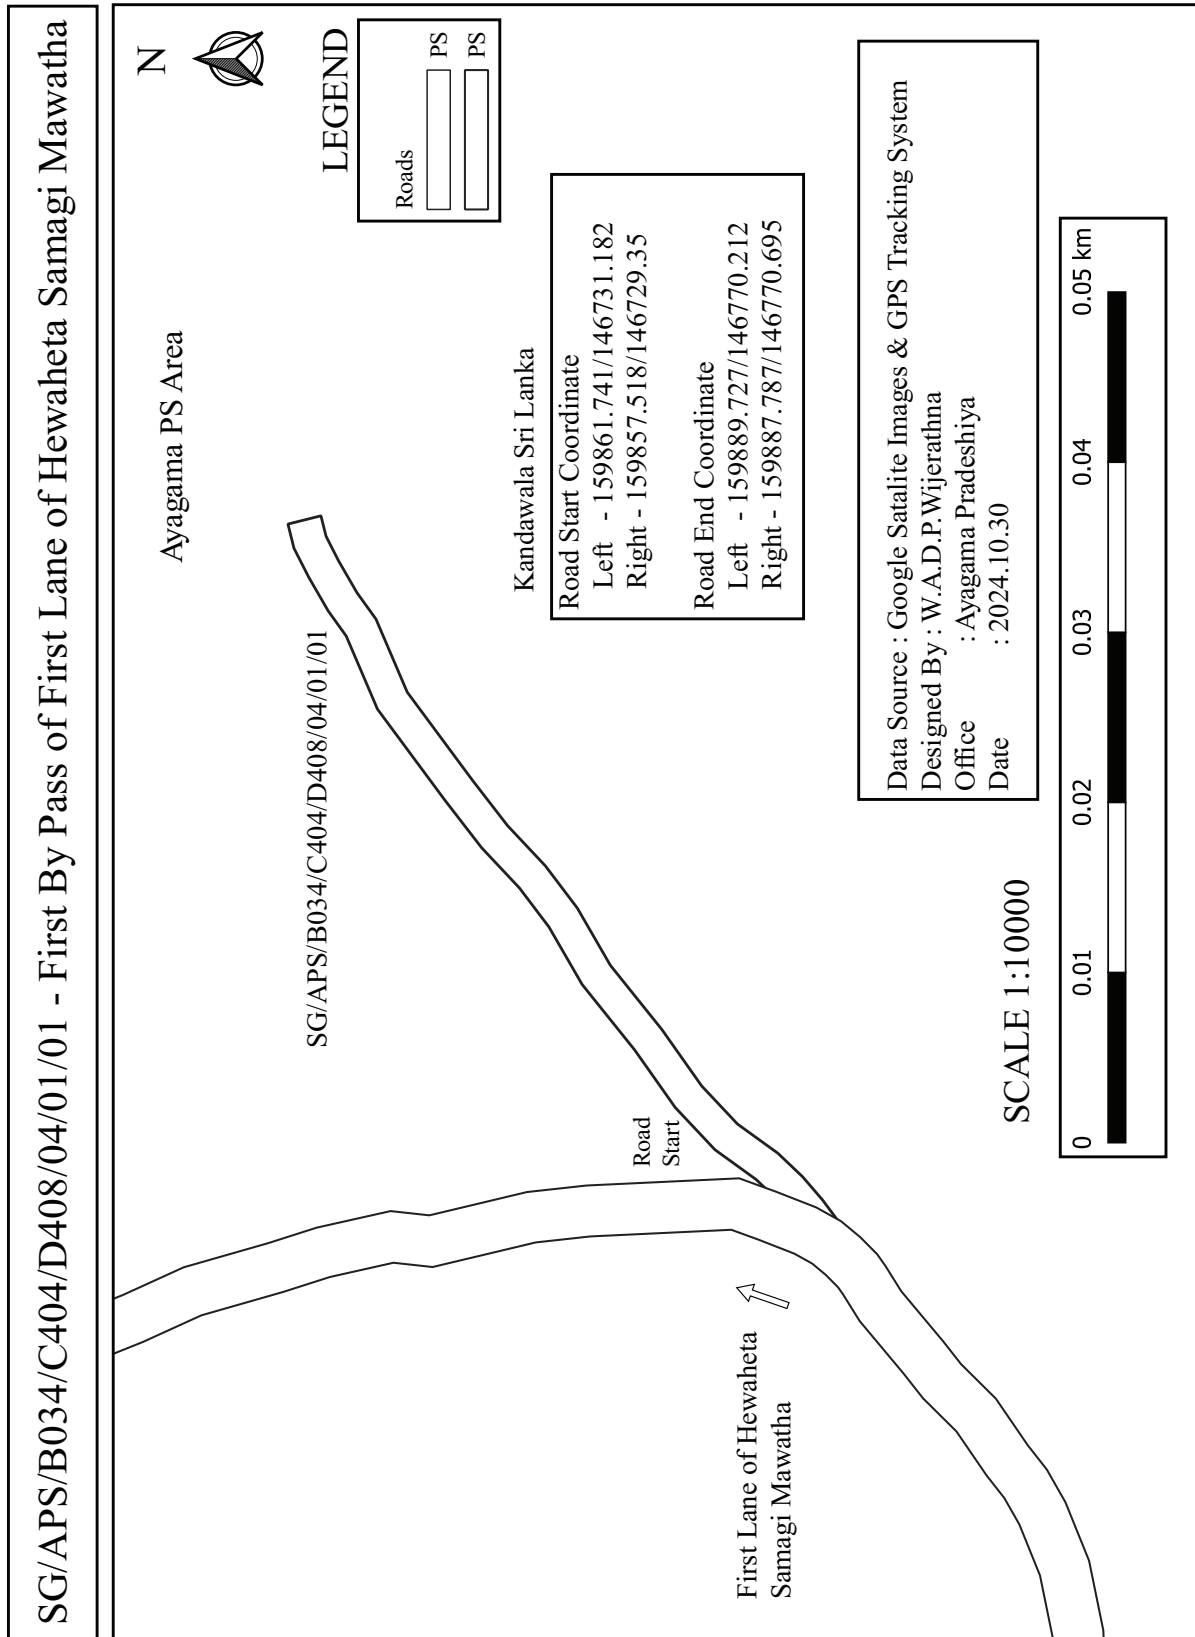

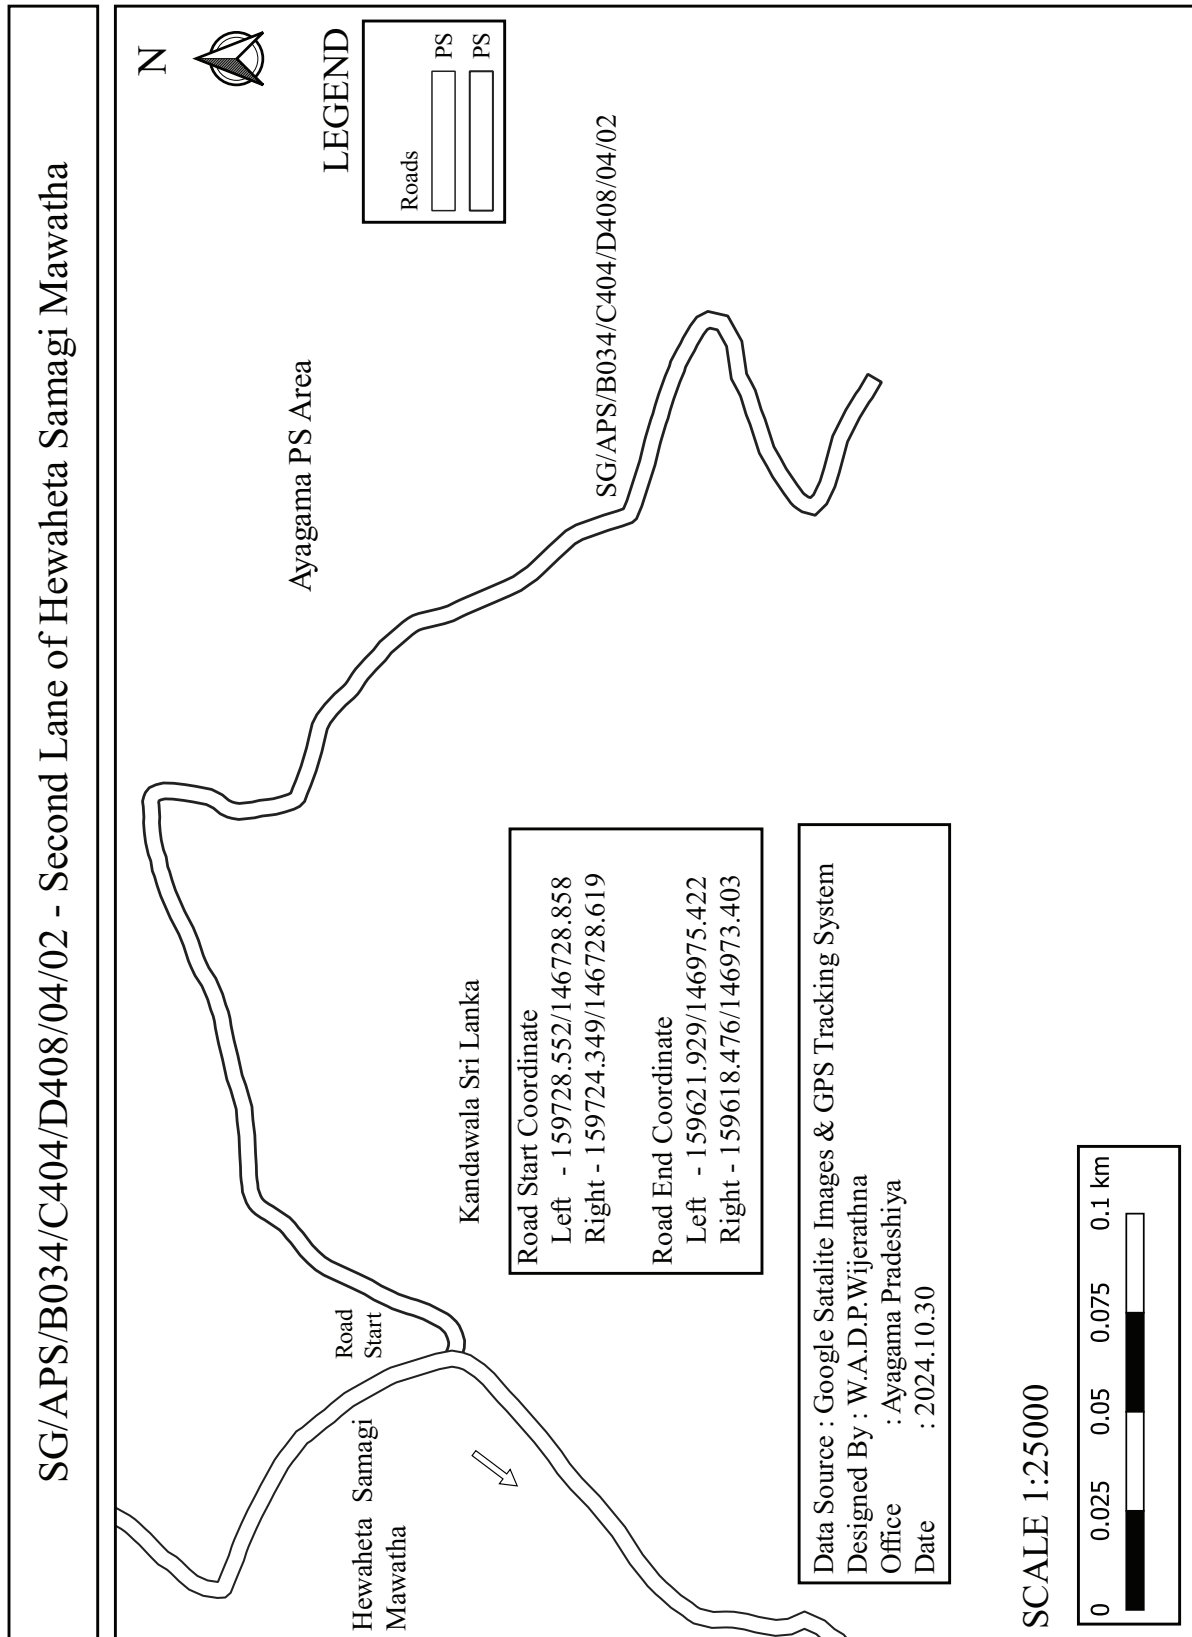


SG/APS/B034/C404/D408/04/02/01 - Footpath - First By Pass Way of Second Lane of Hewaheta Samagi Mawatha

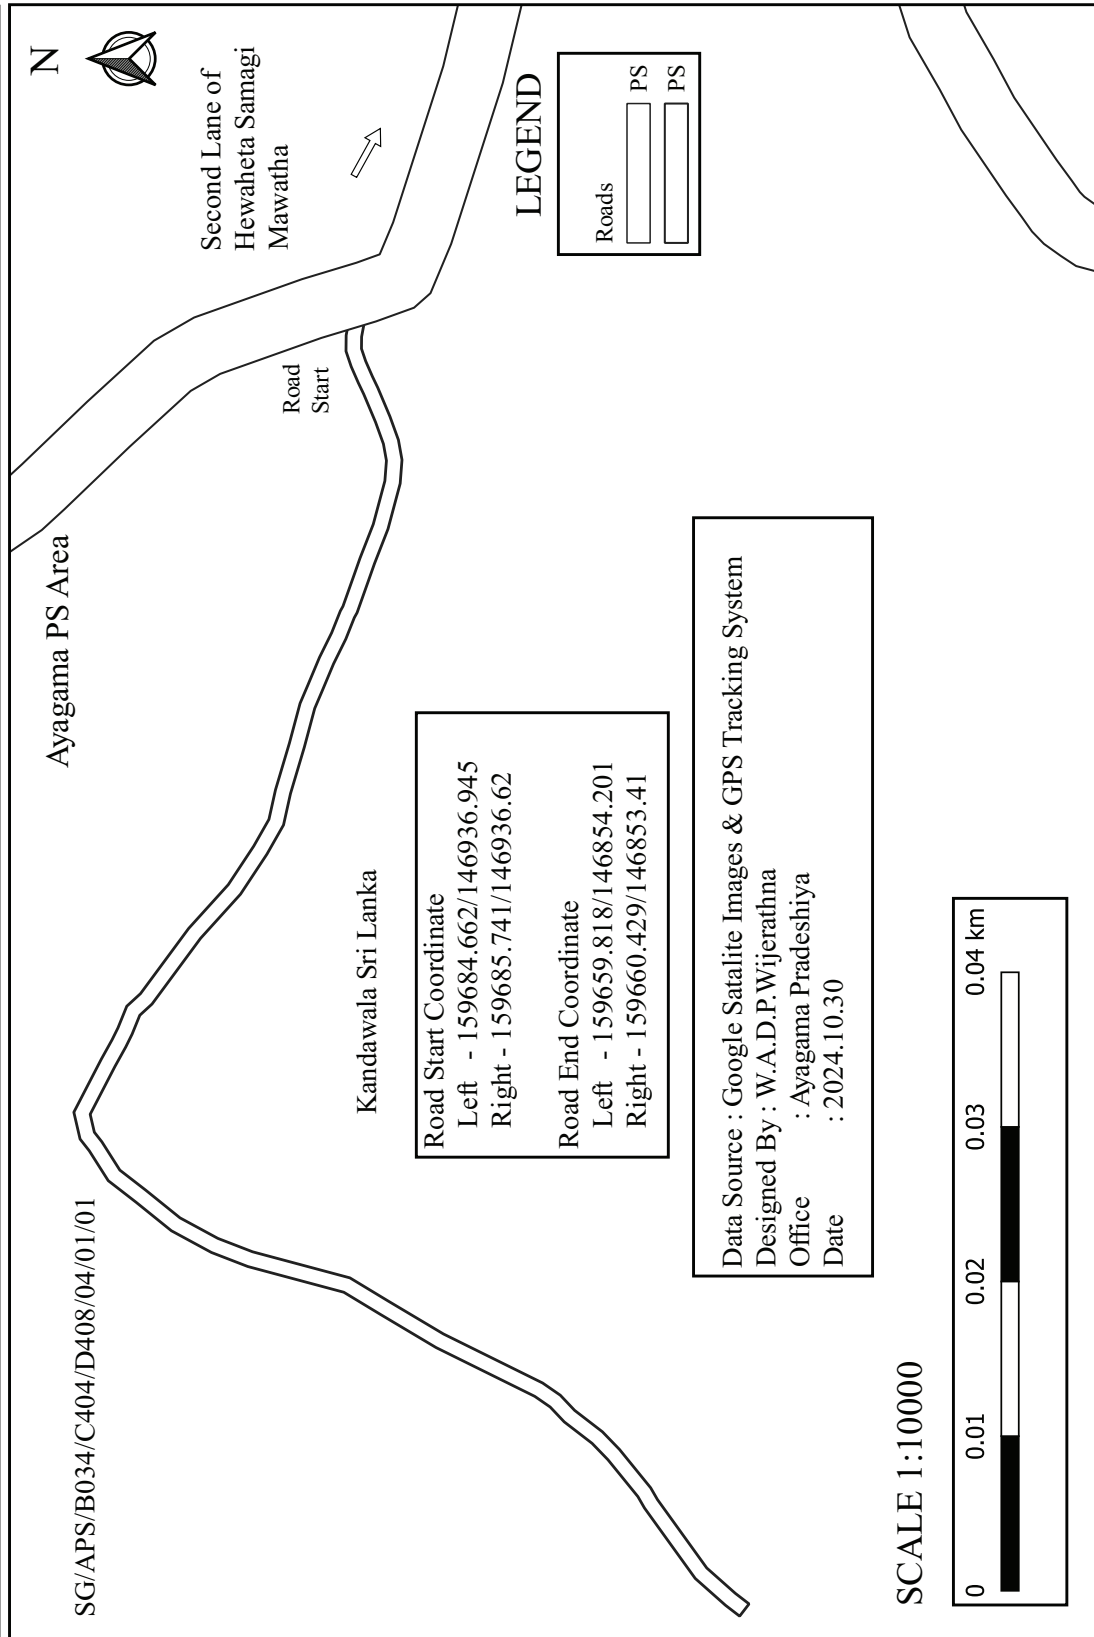


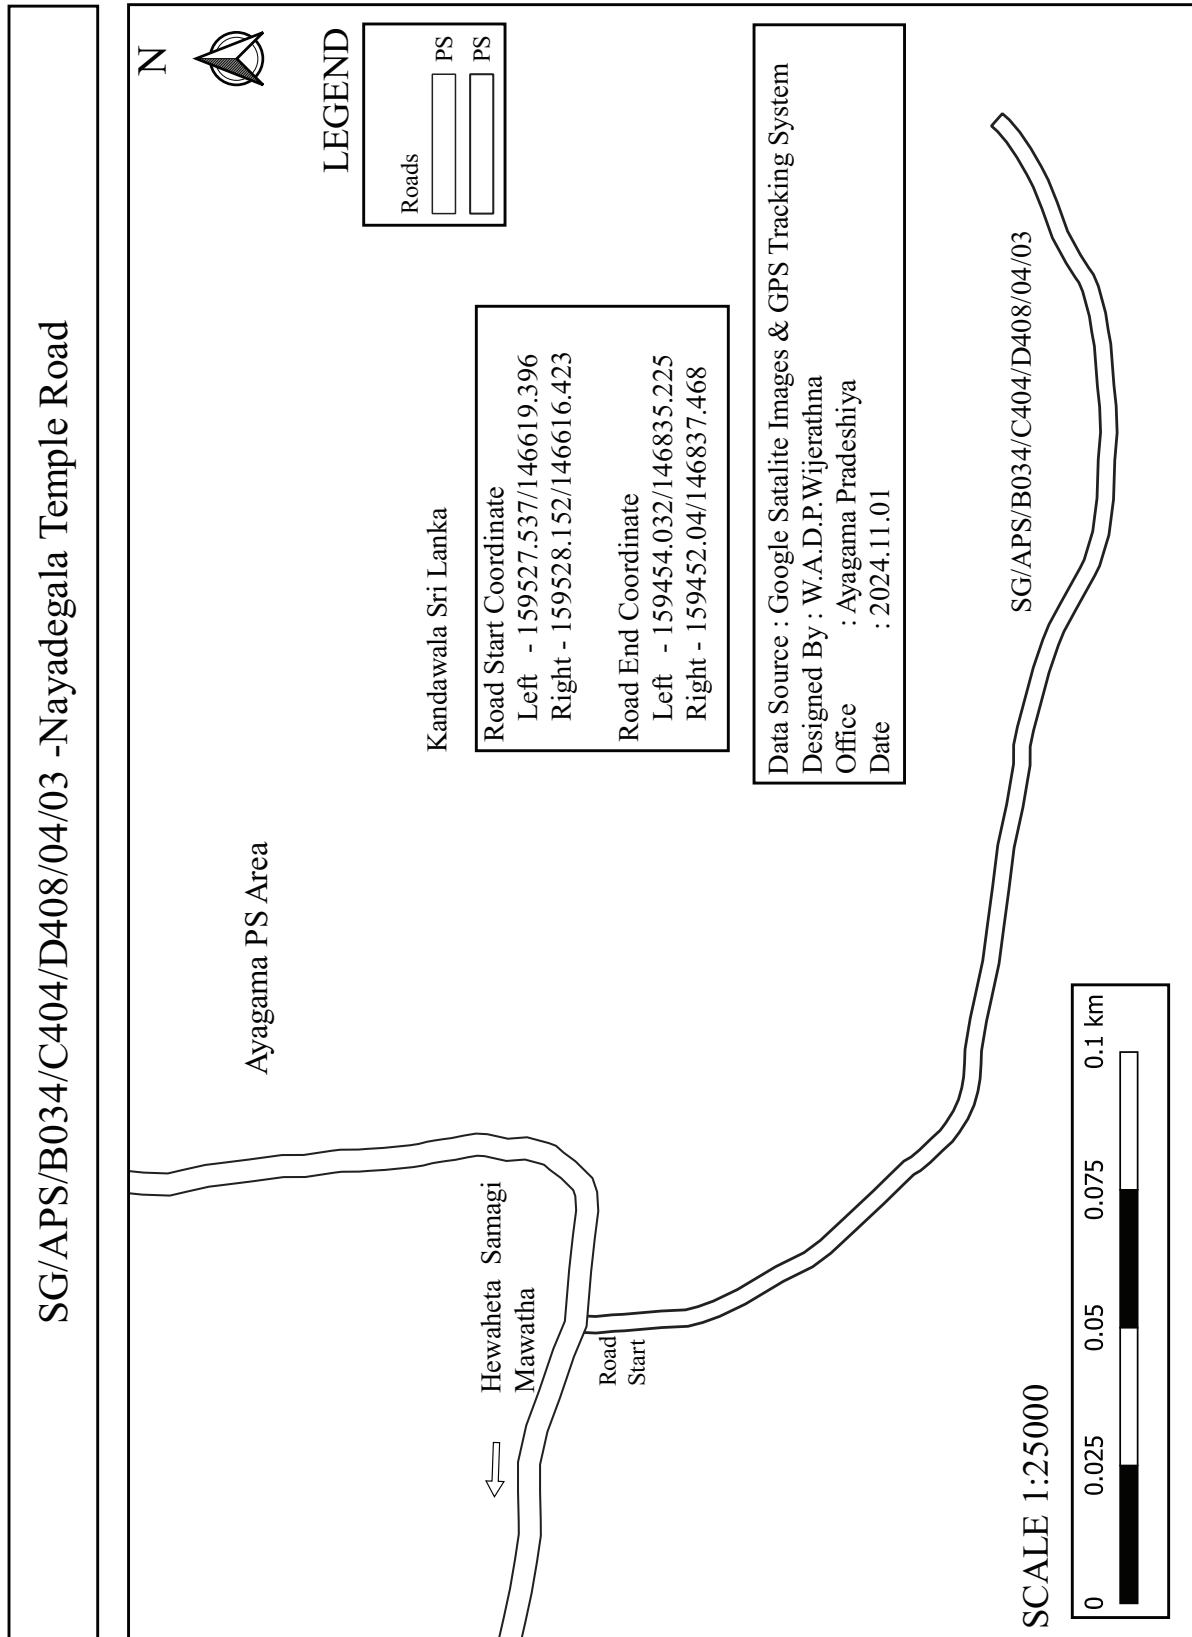



SG/APS/B034/C404/D408/06 - First Lane of Pitakanda Tea Colony Road

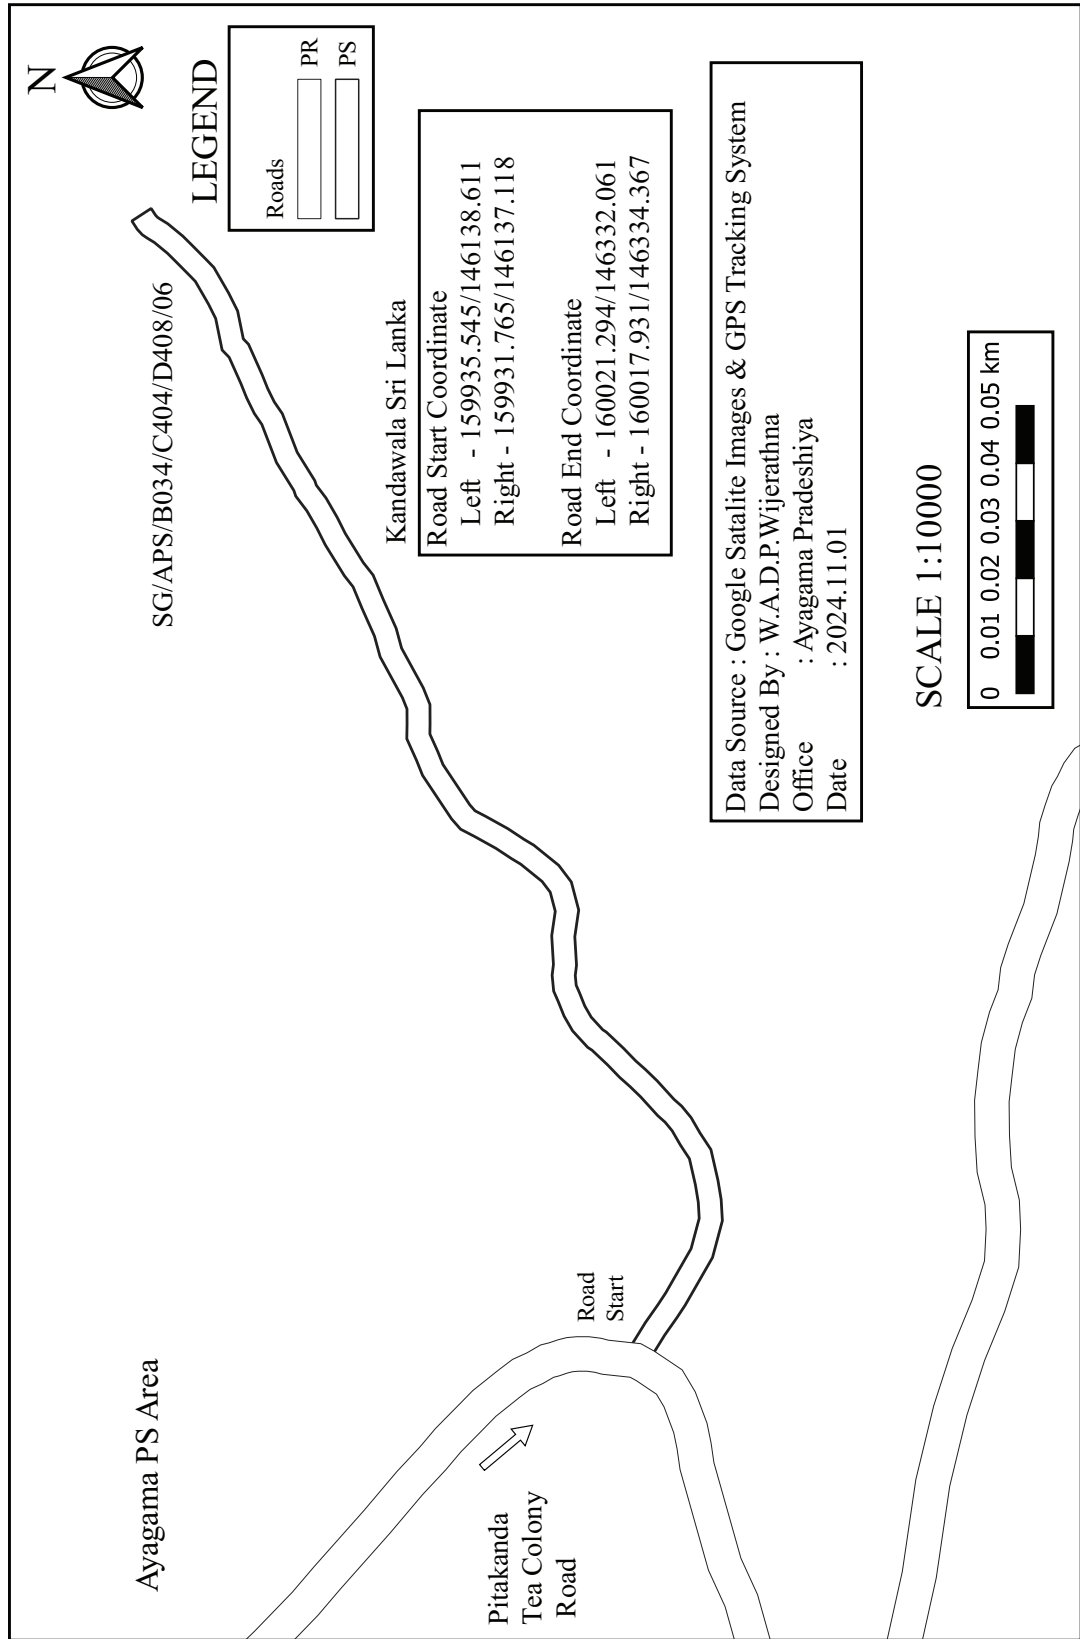



SG/APS/B034/C404/D408/07 - Second Lane of Pitakanda Tea Colony Road

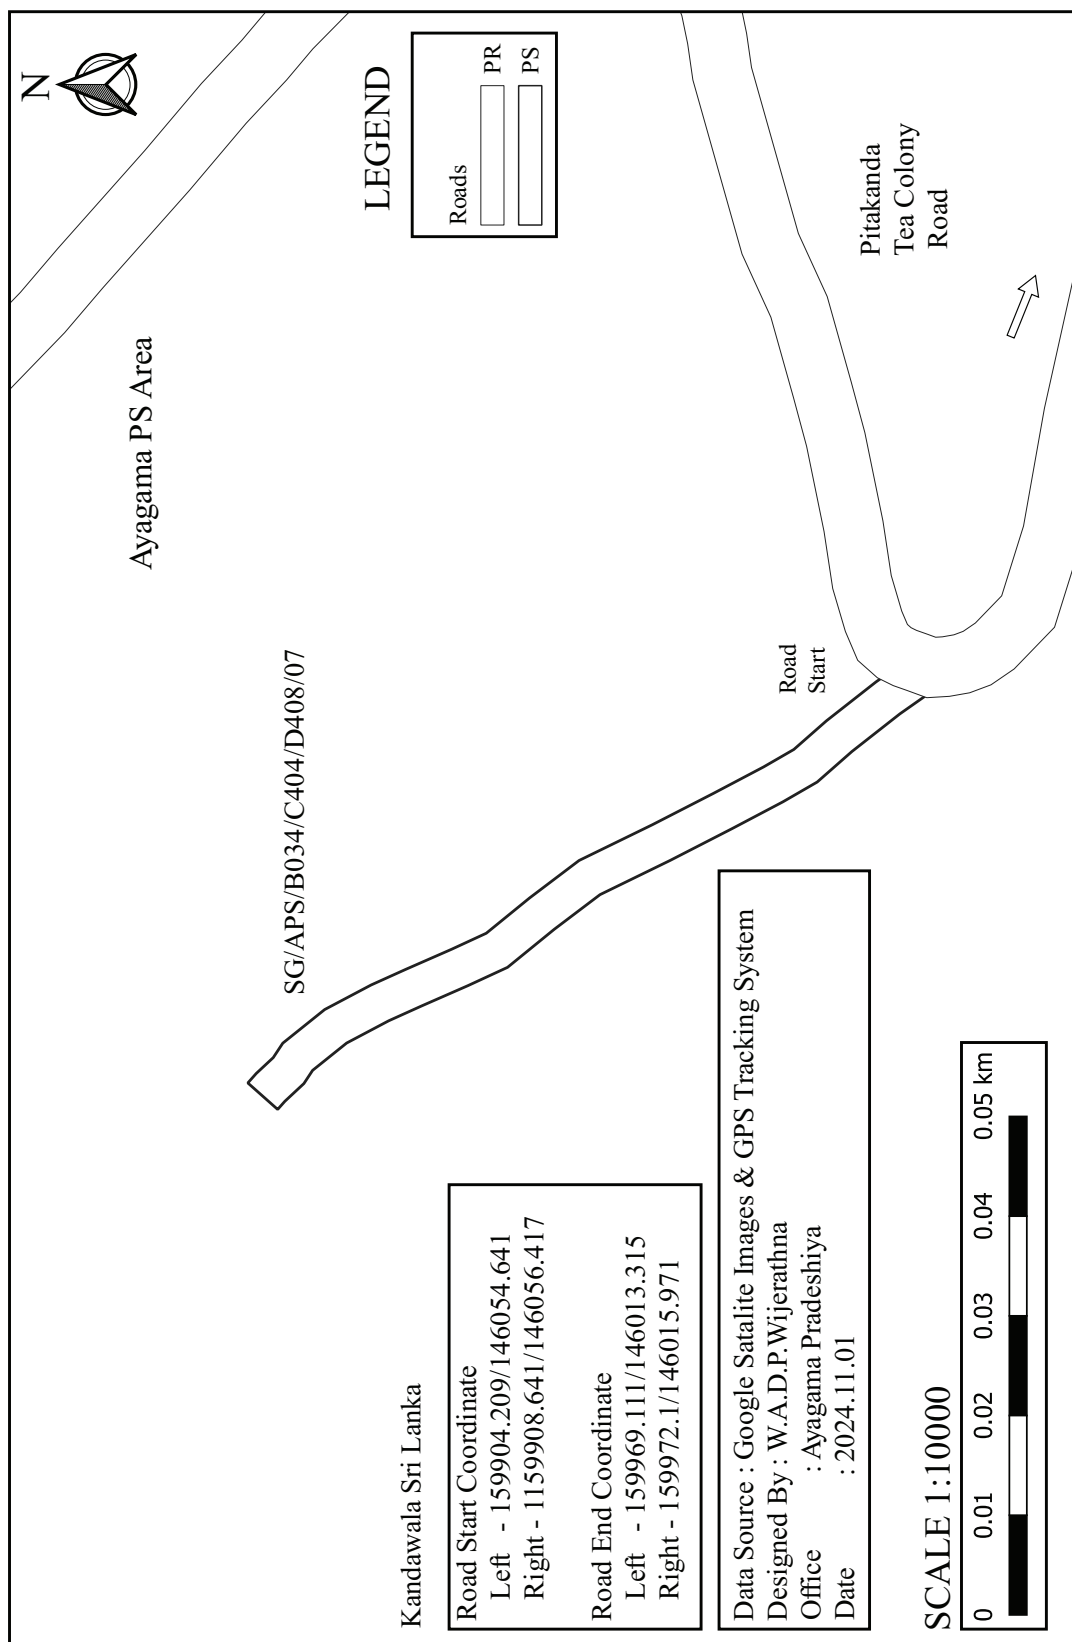


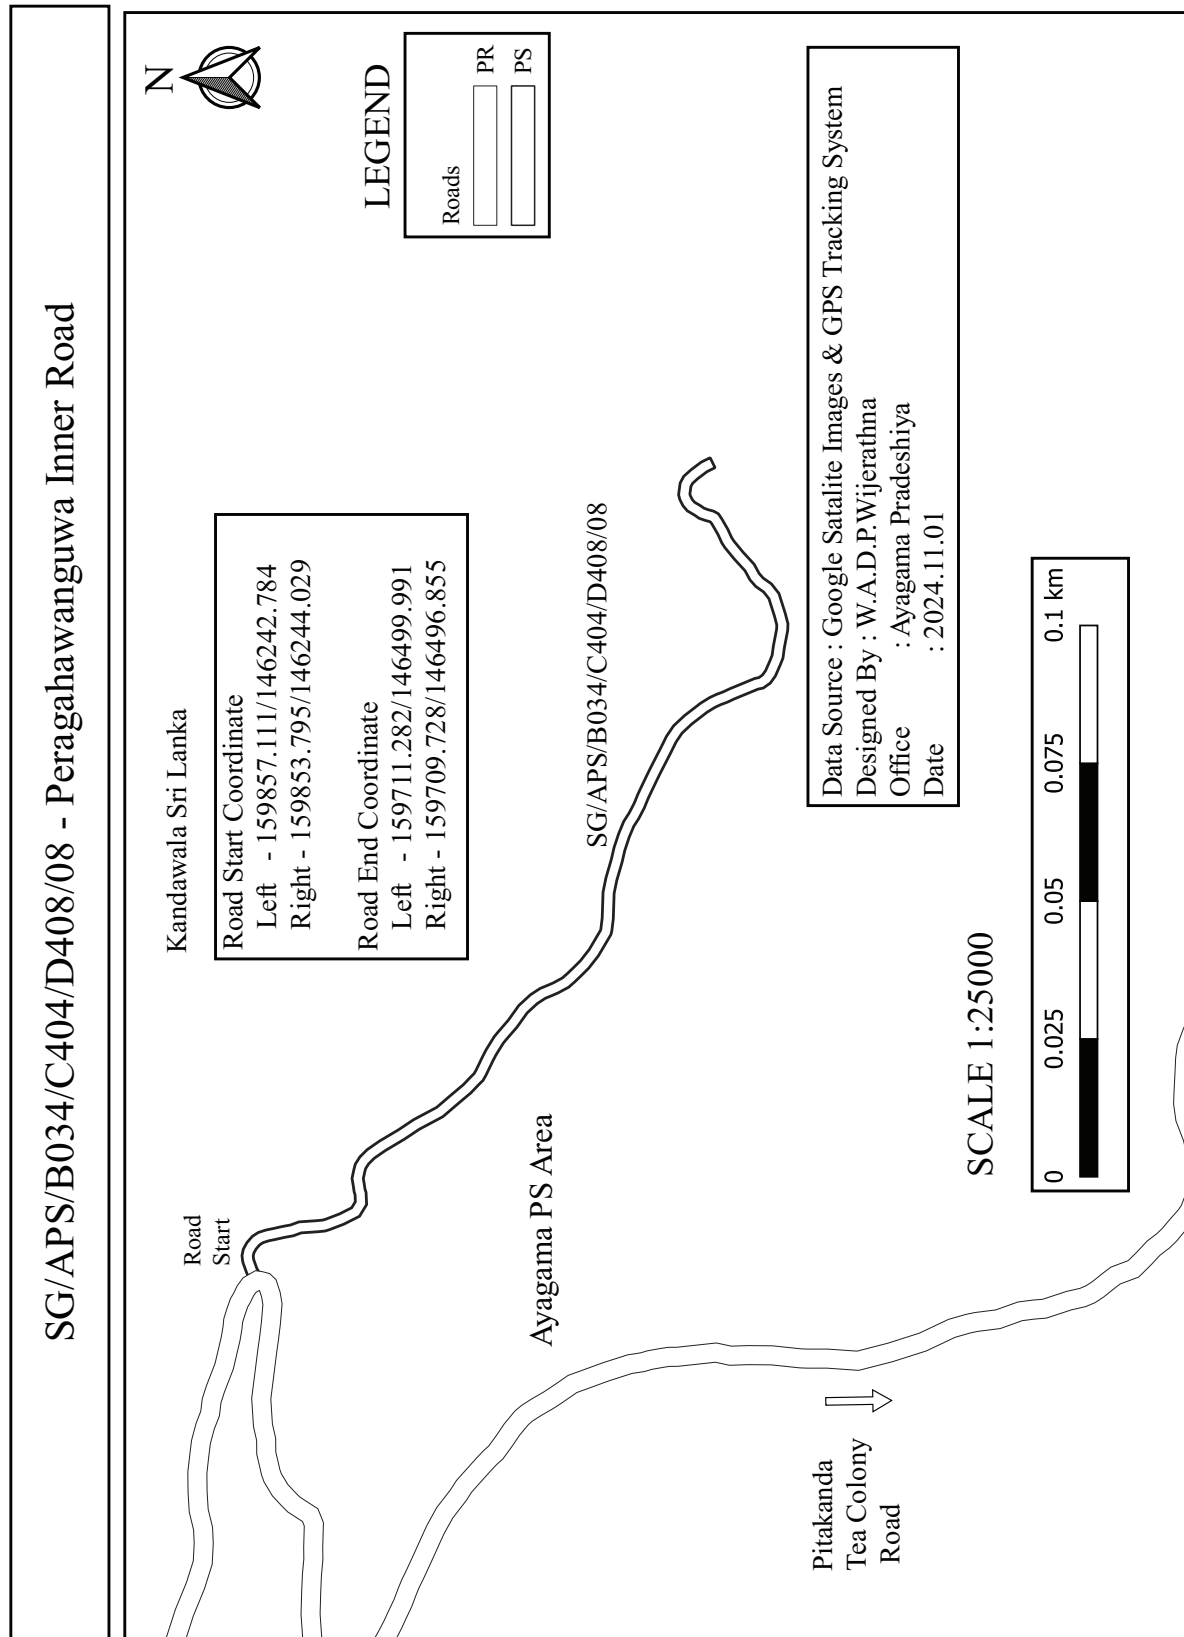


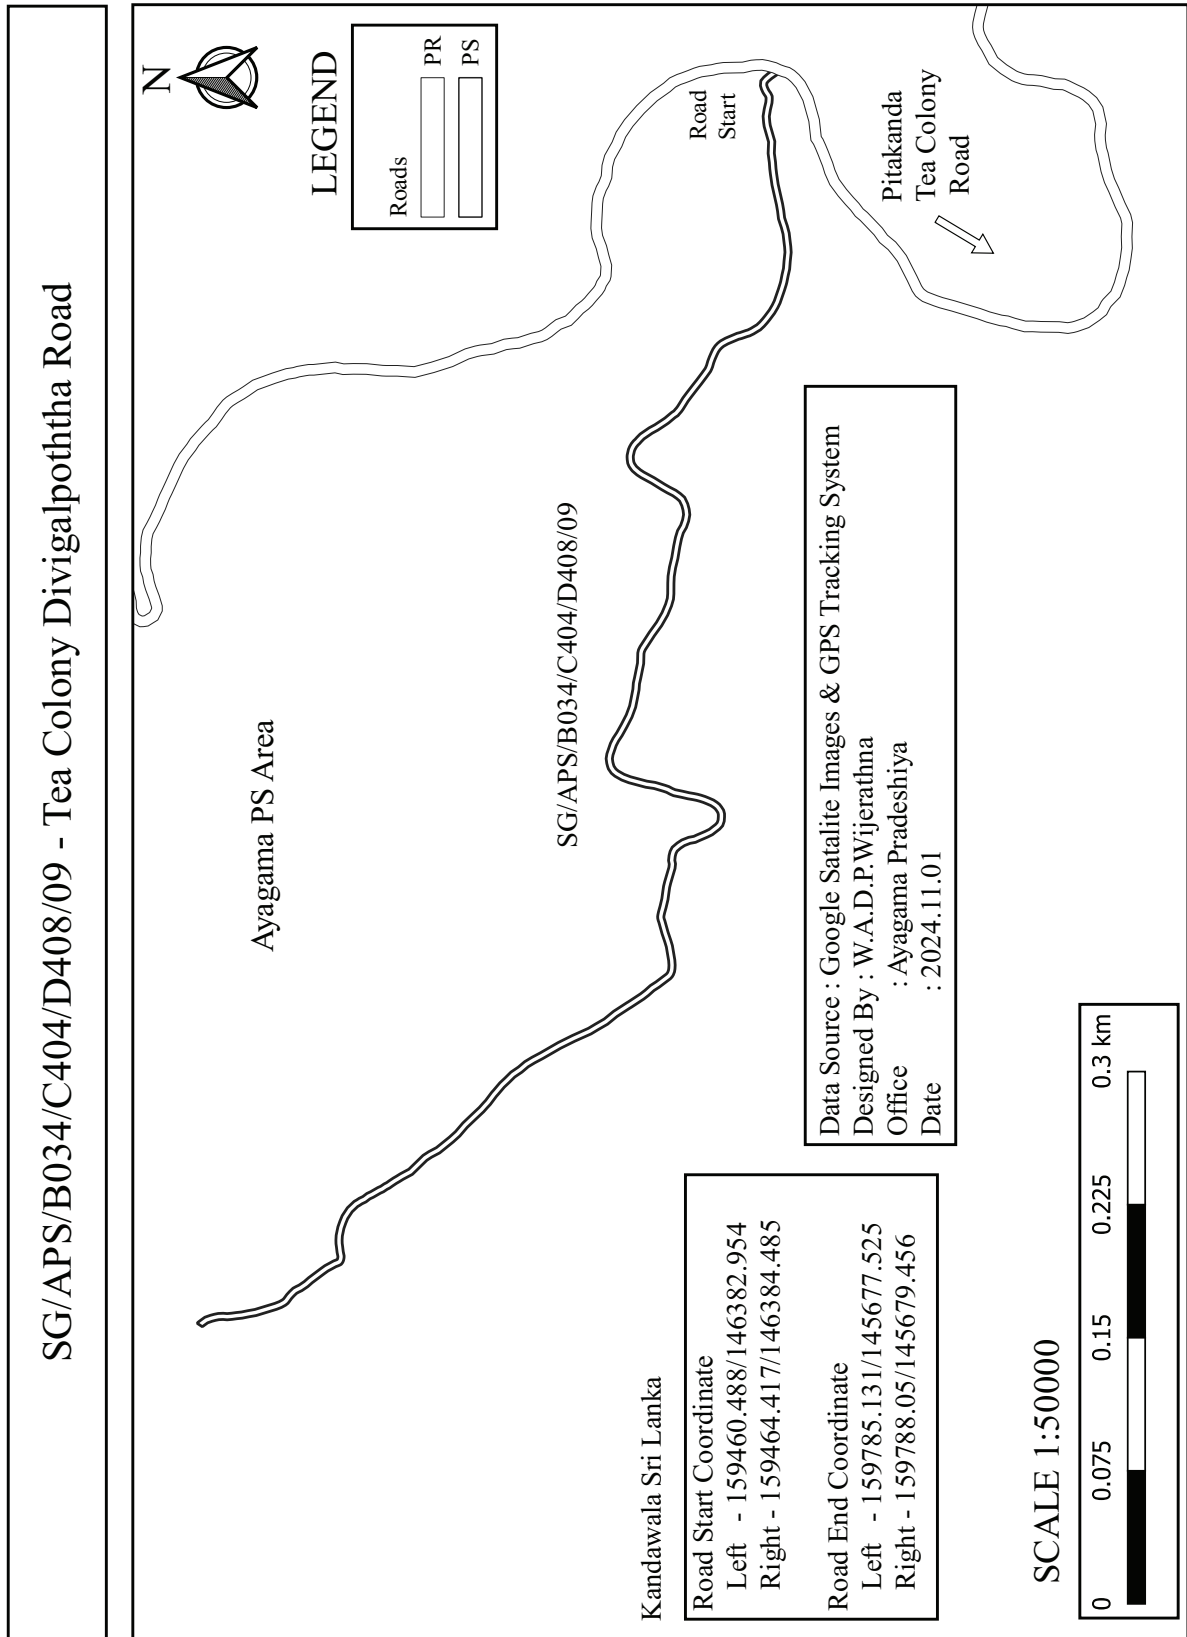


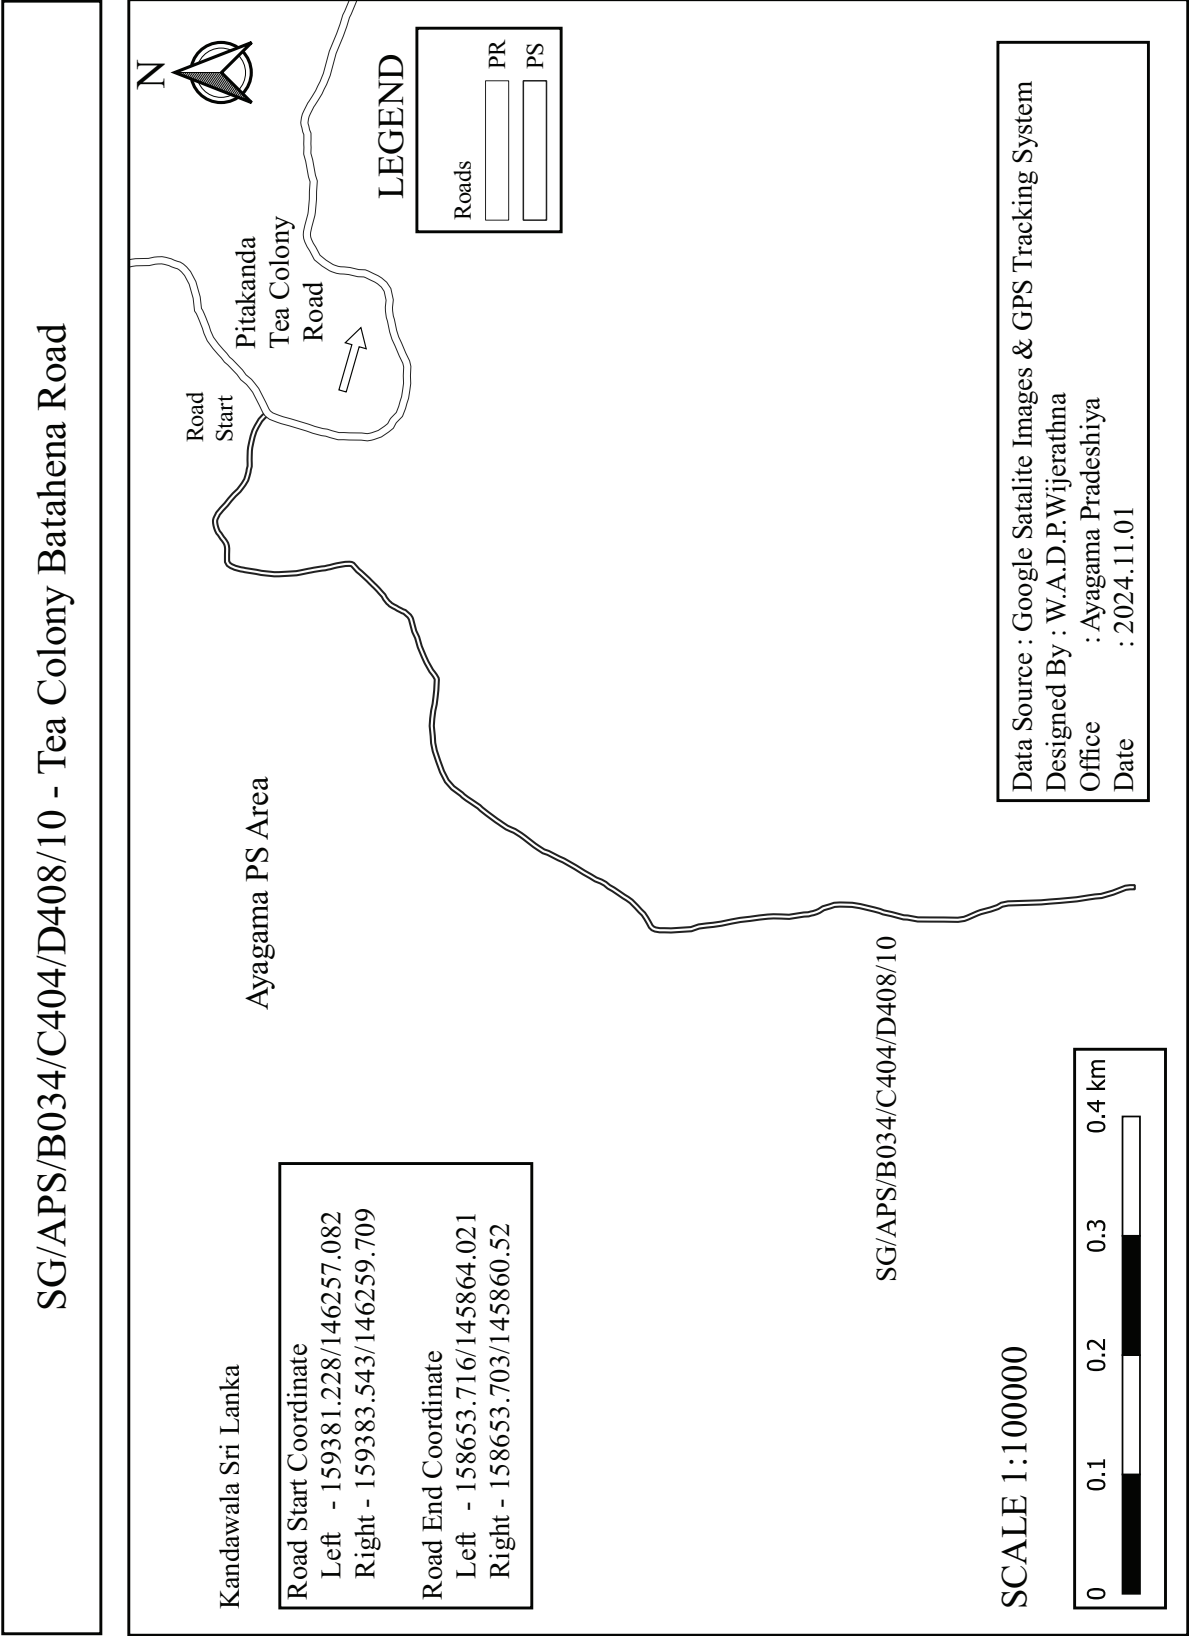


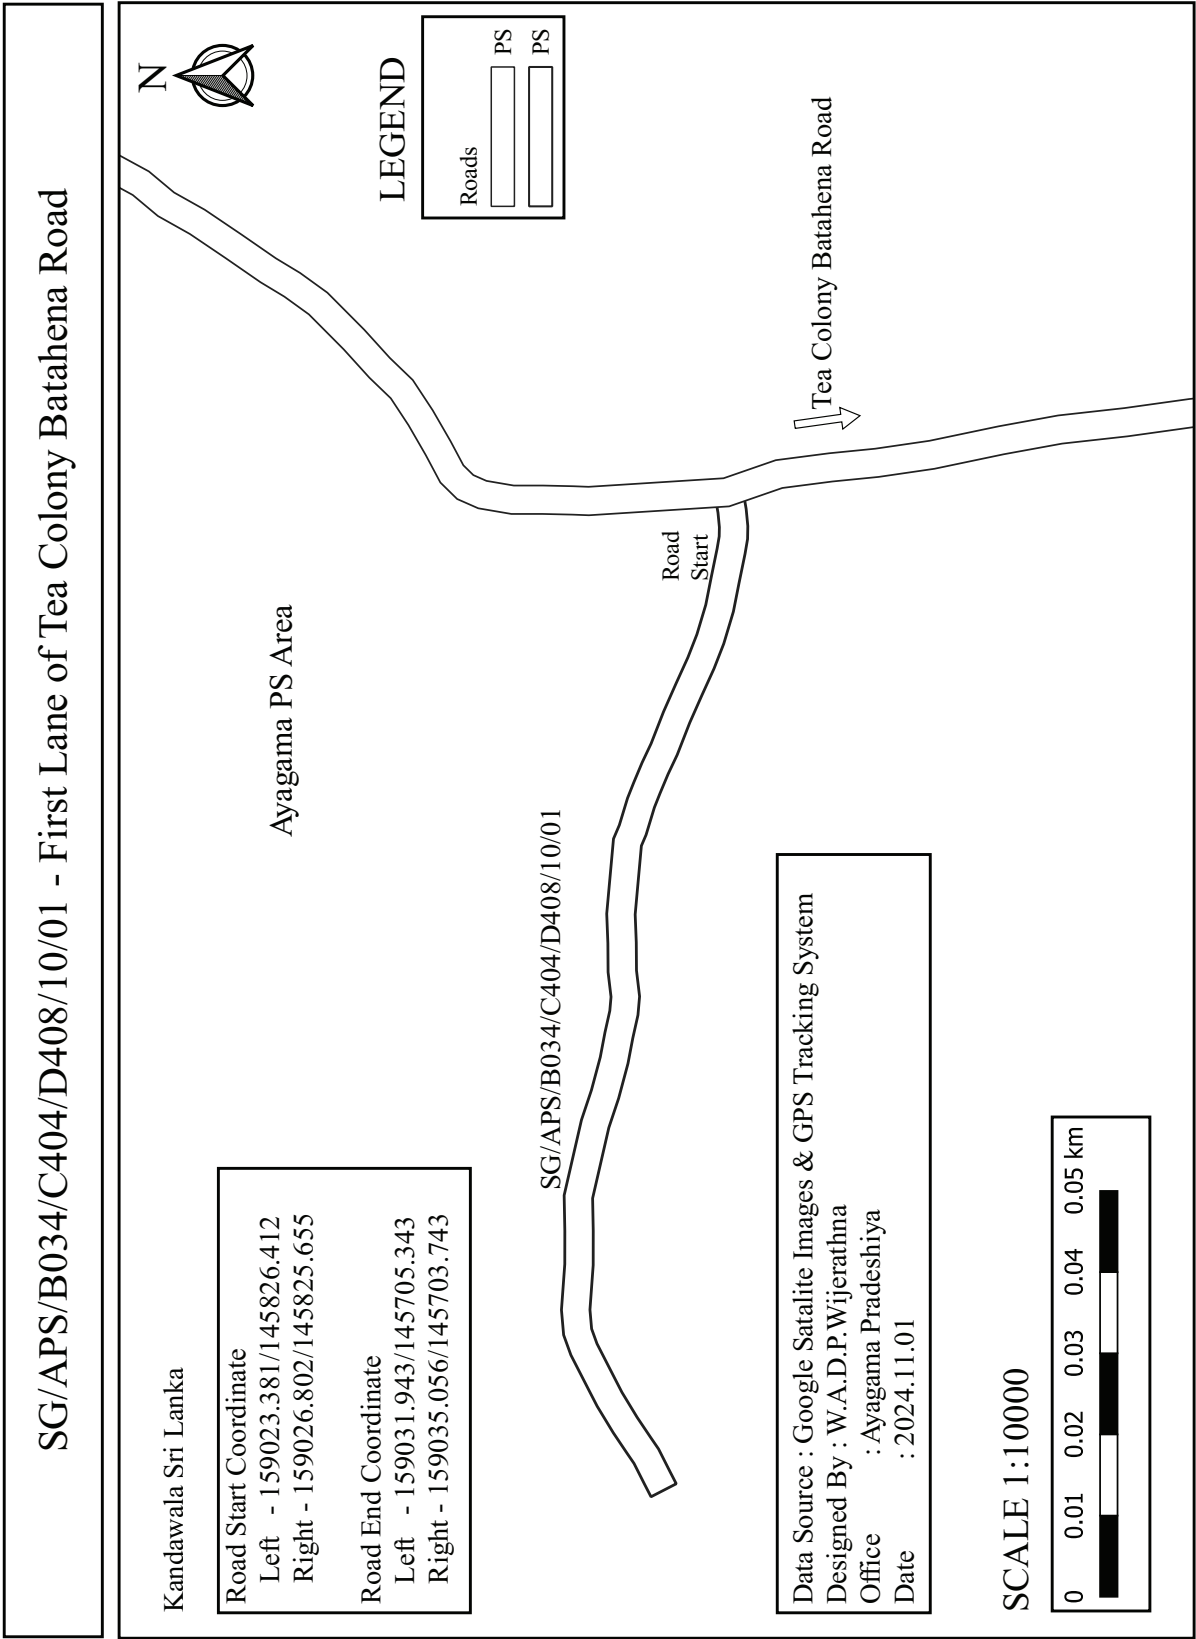


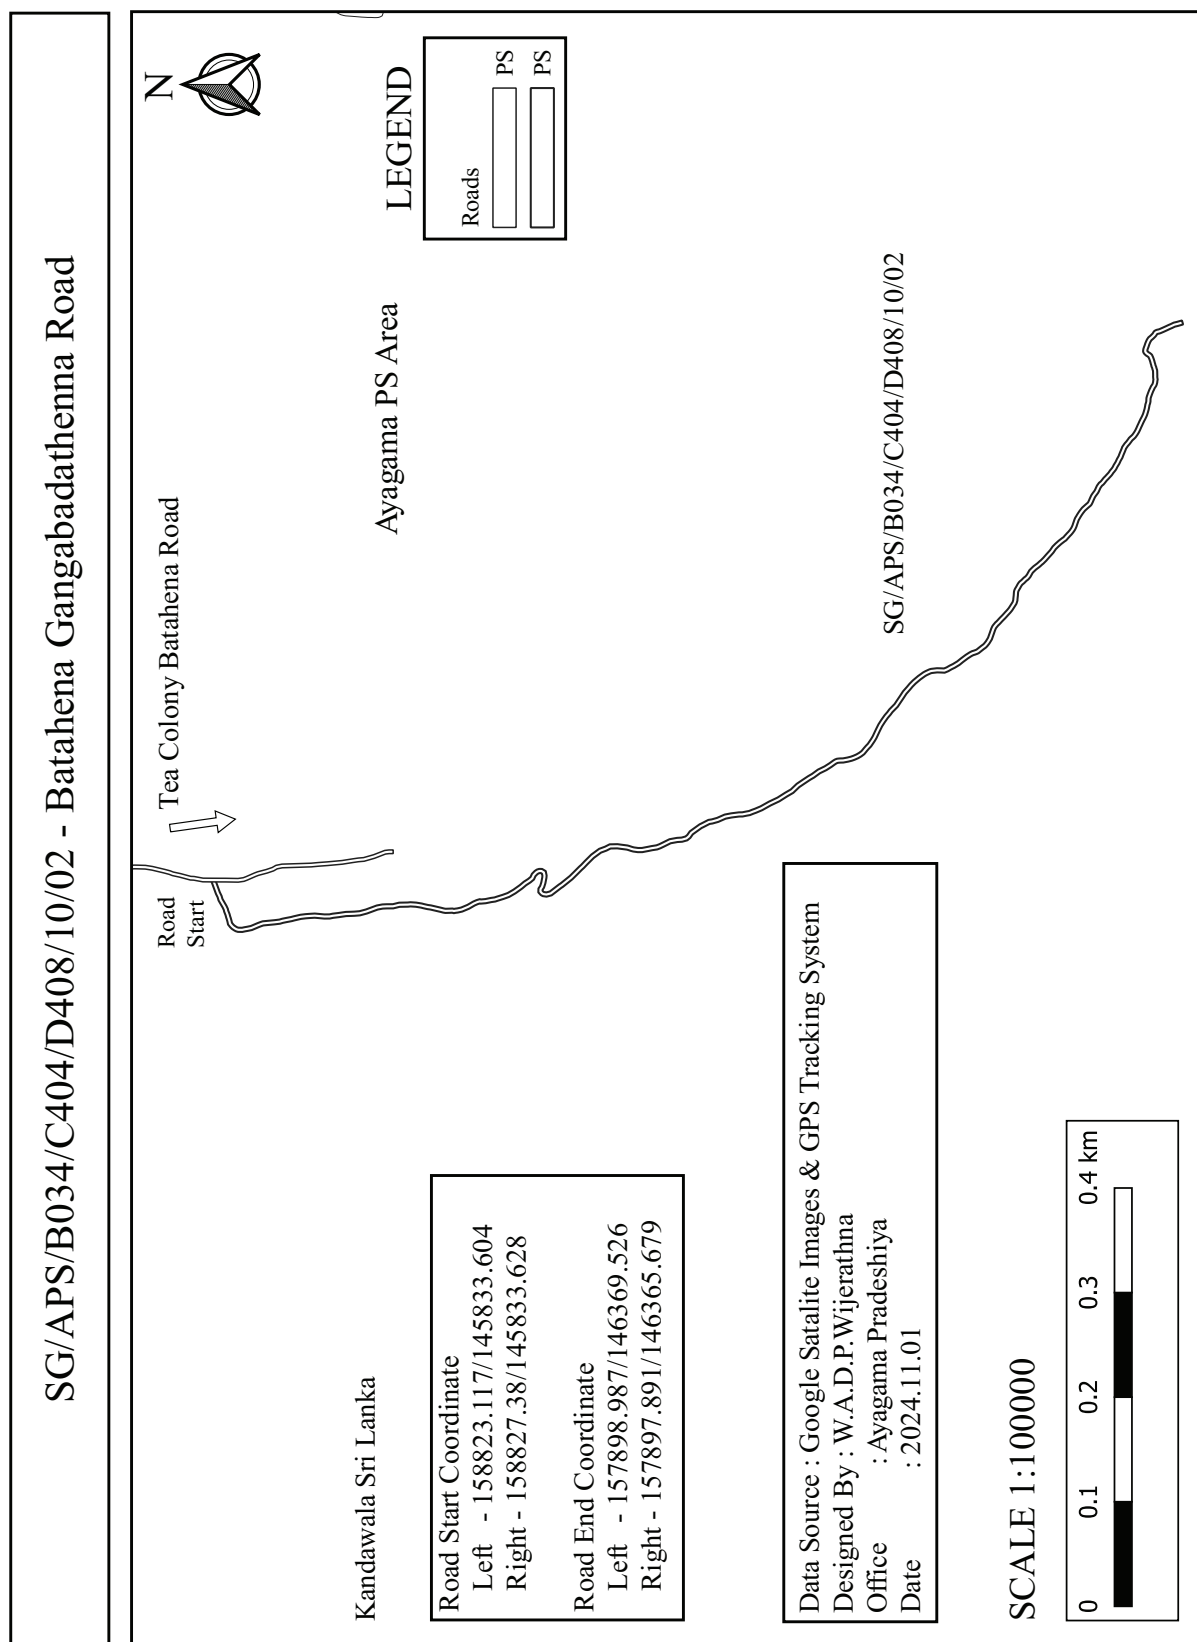


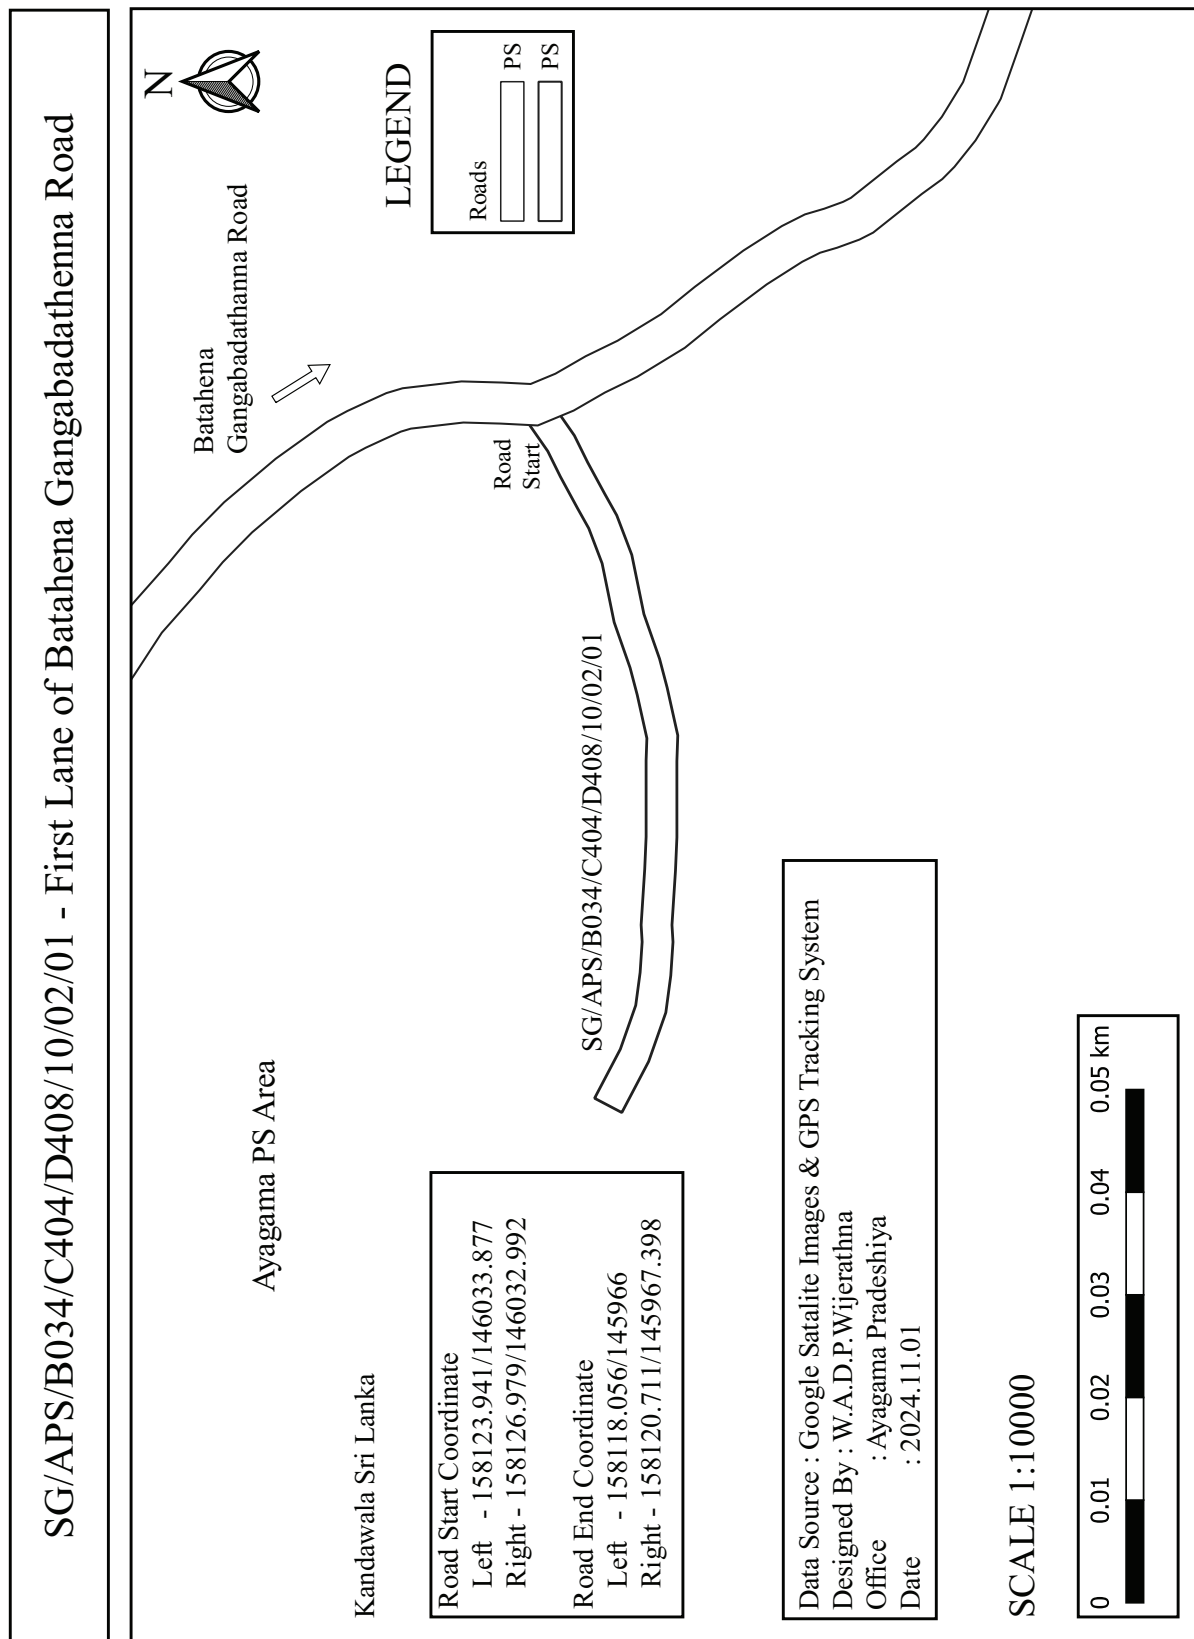


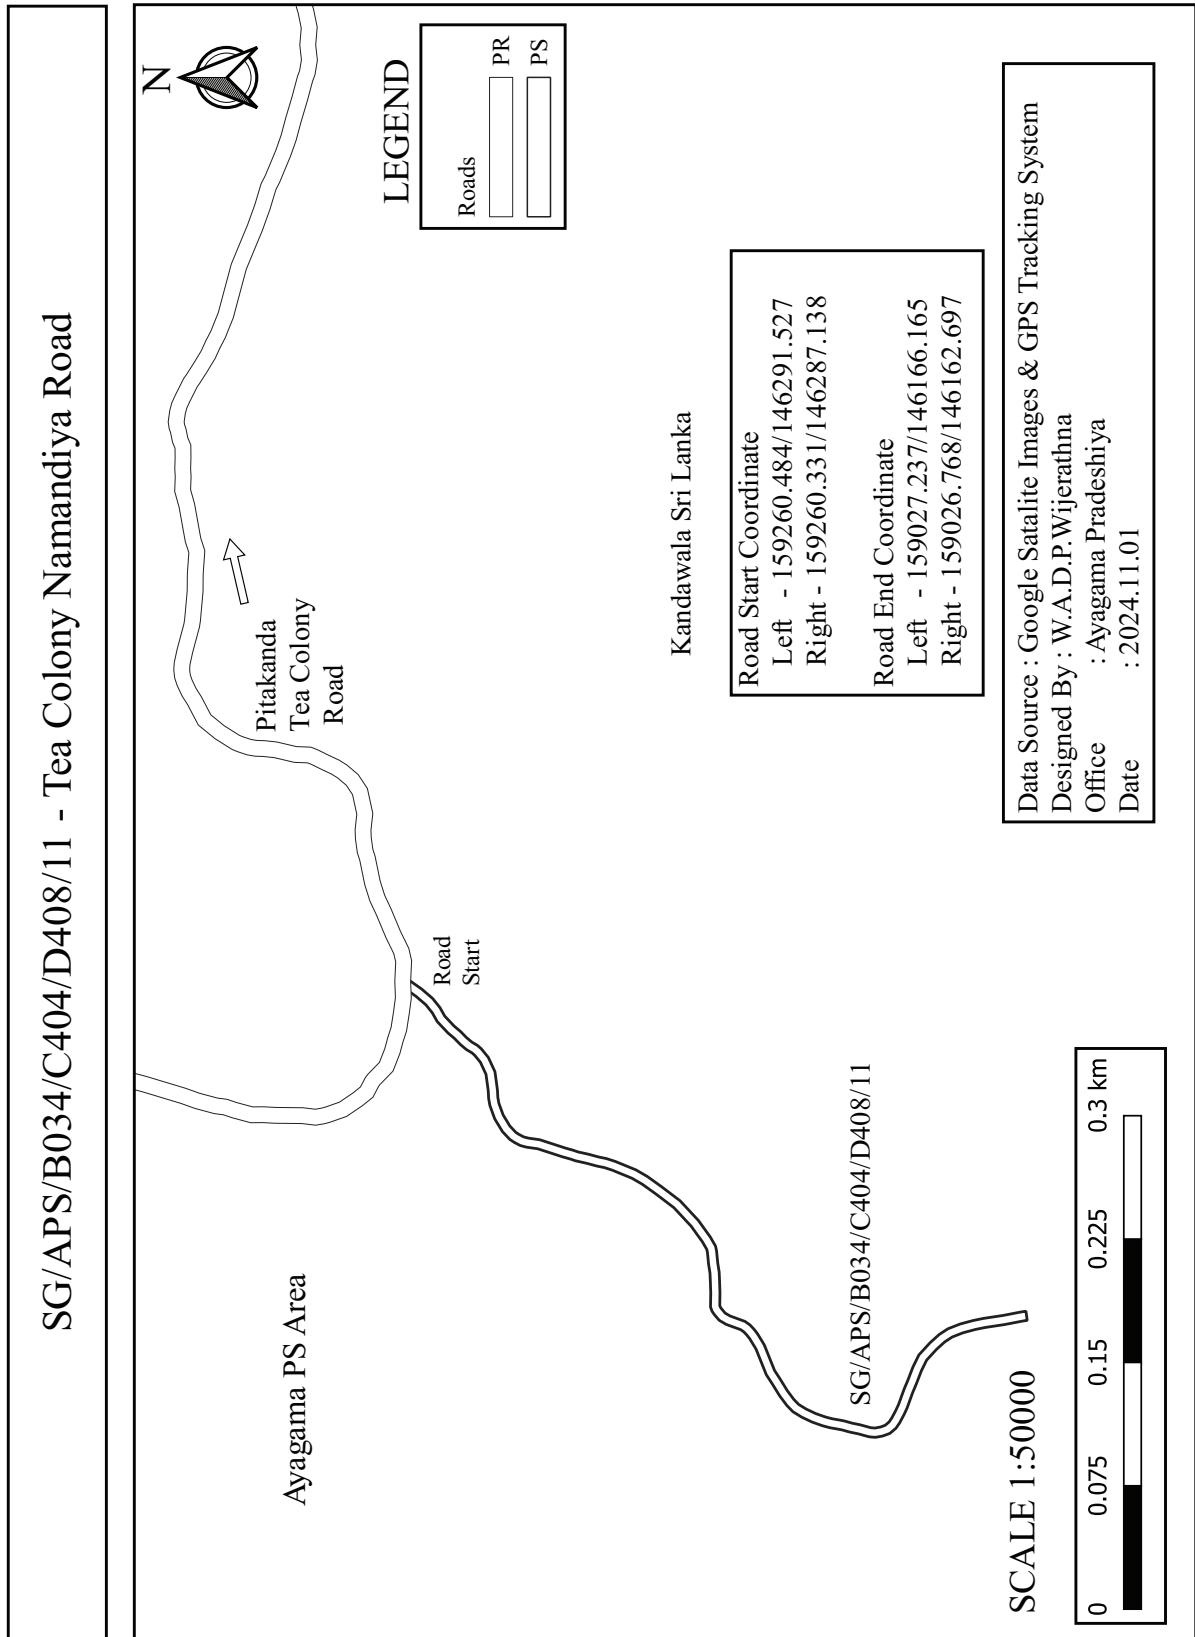


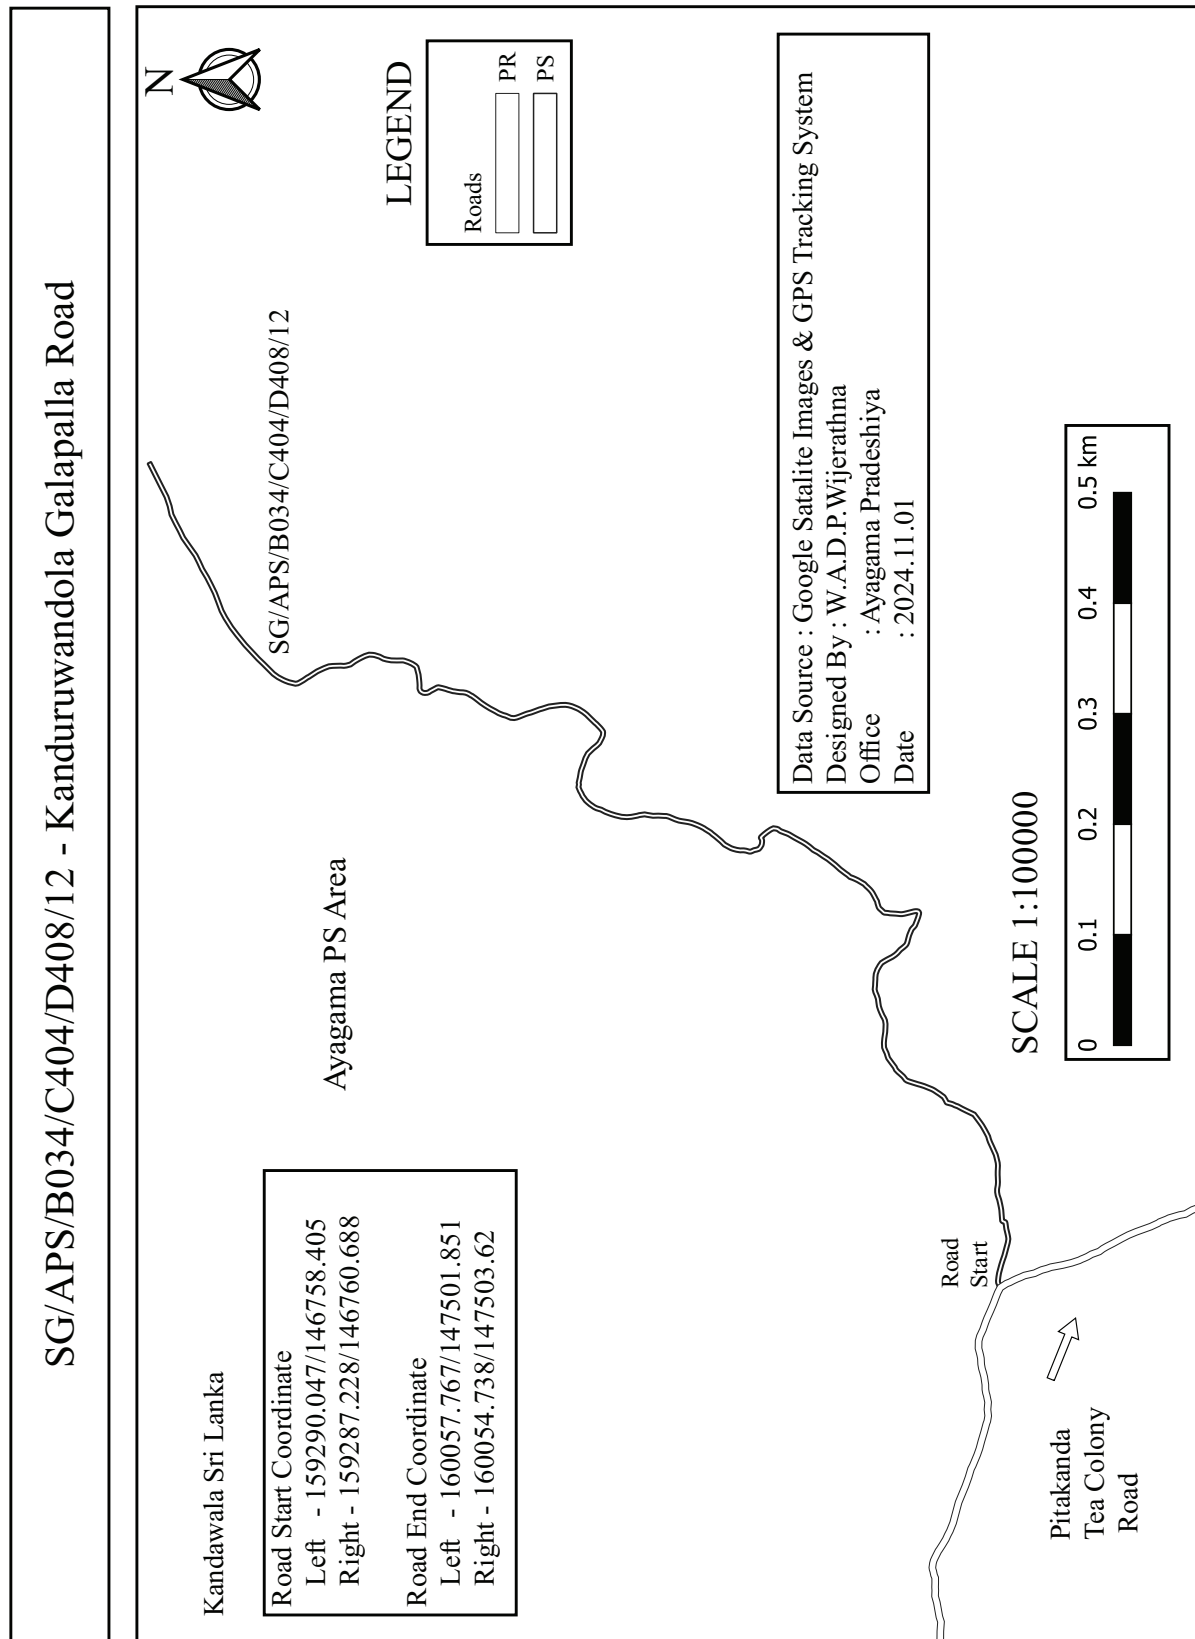


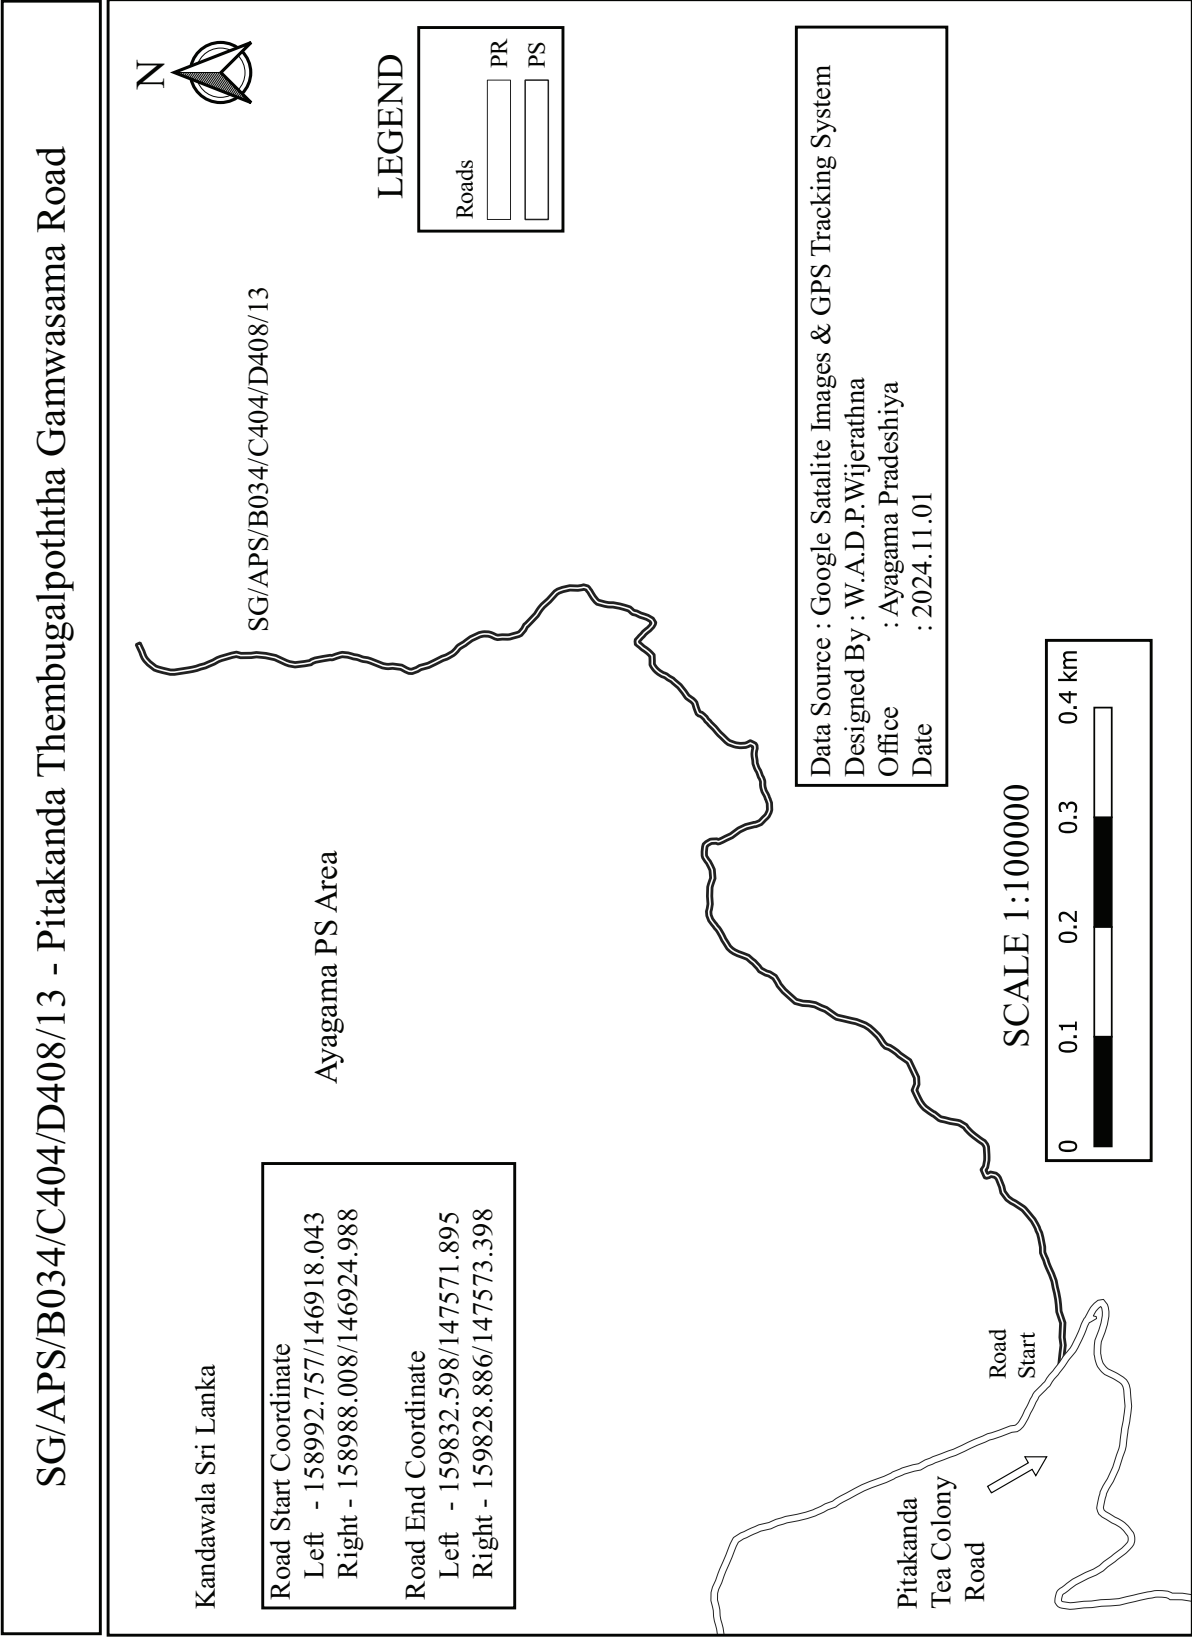


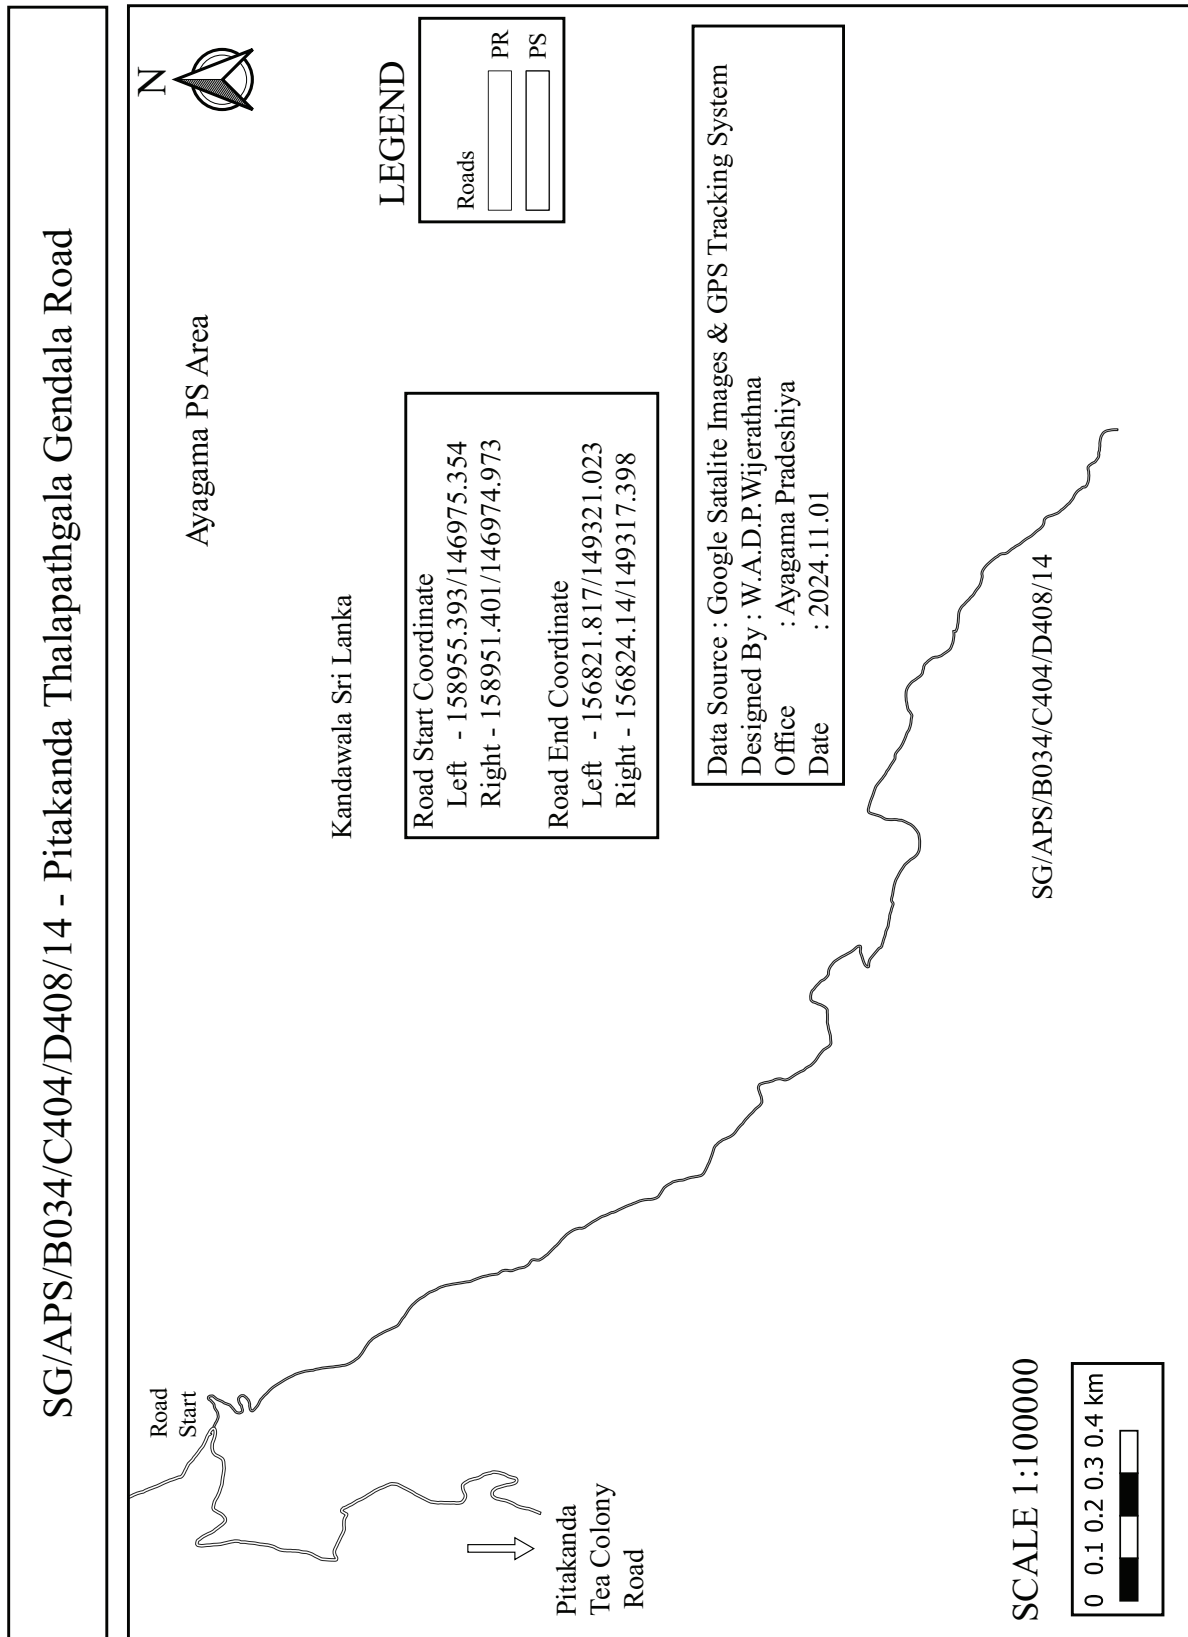


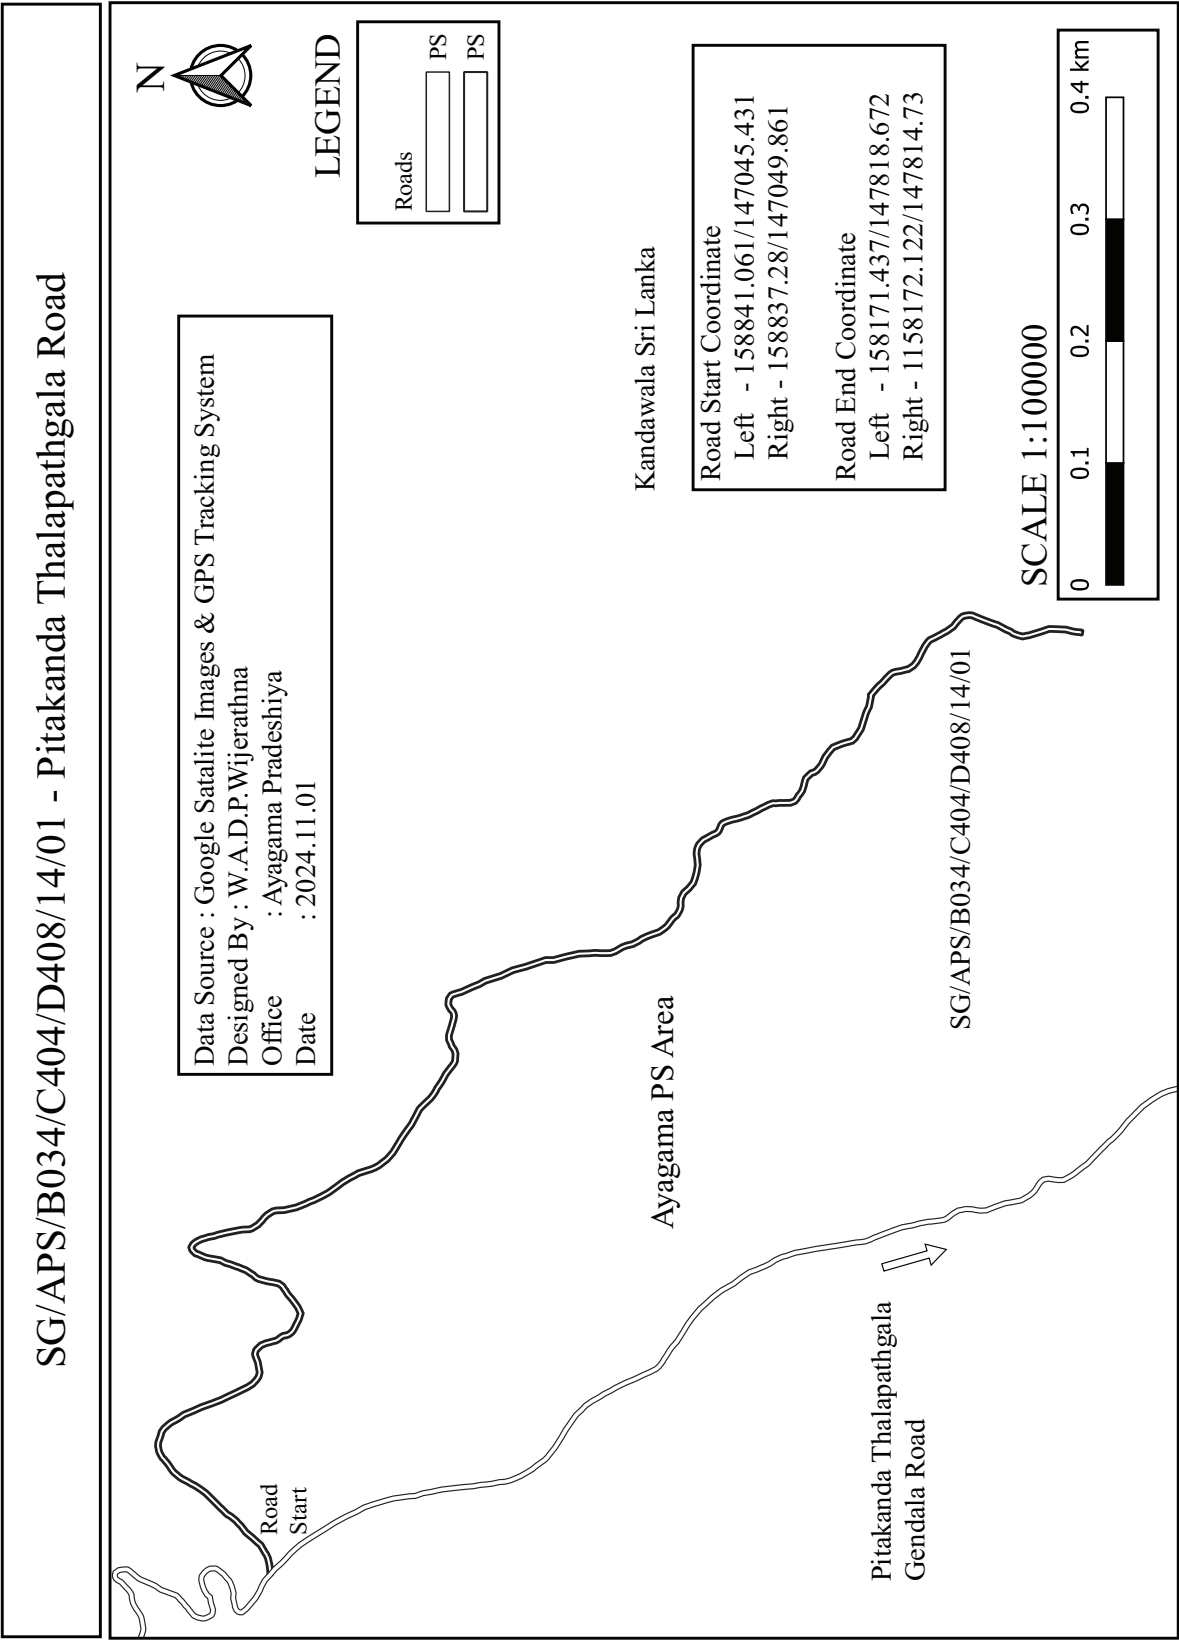


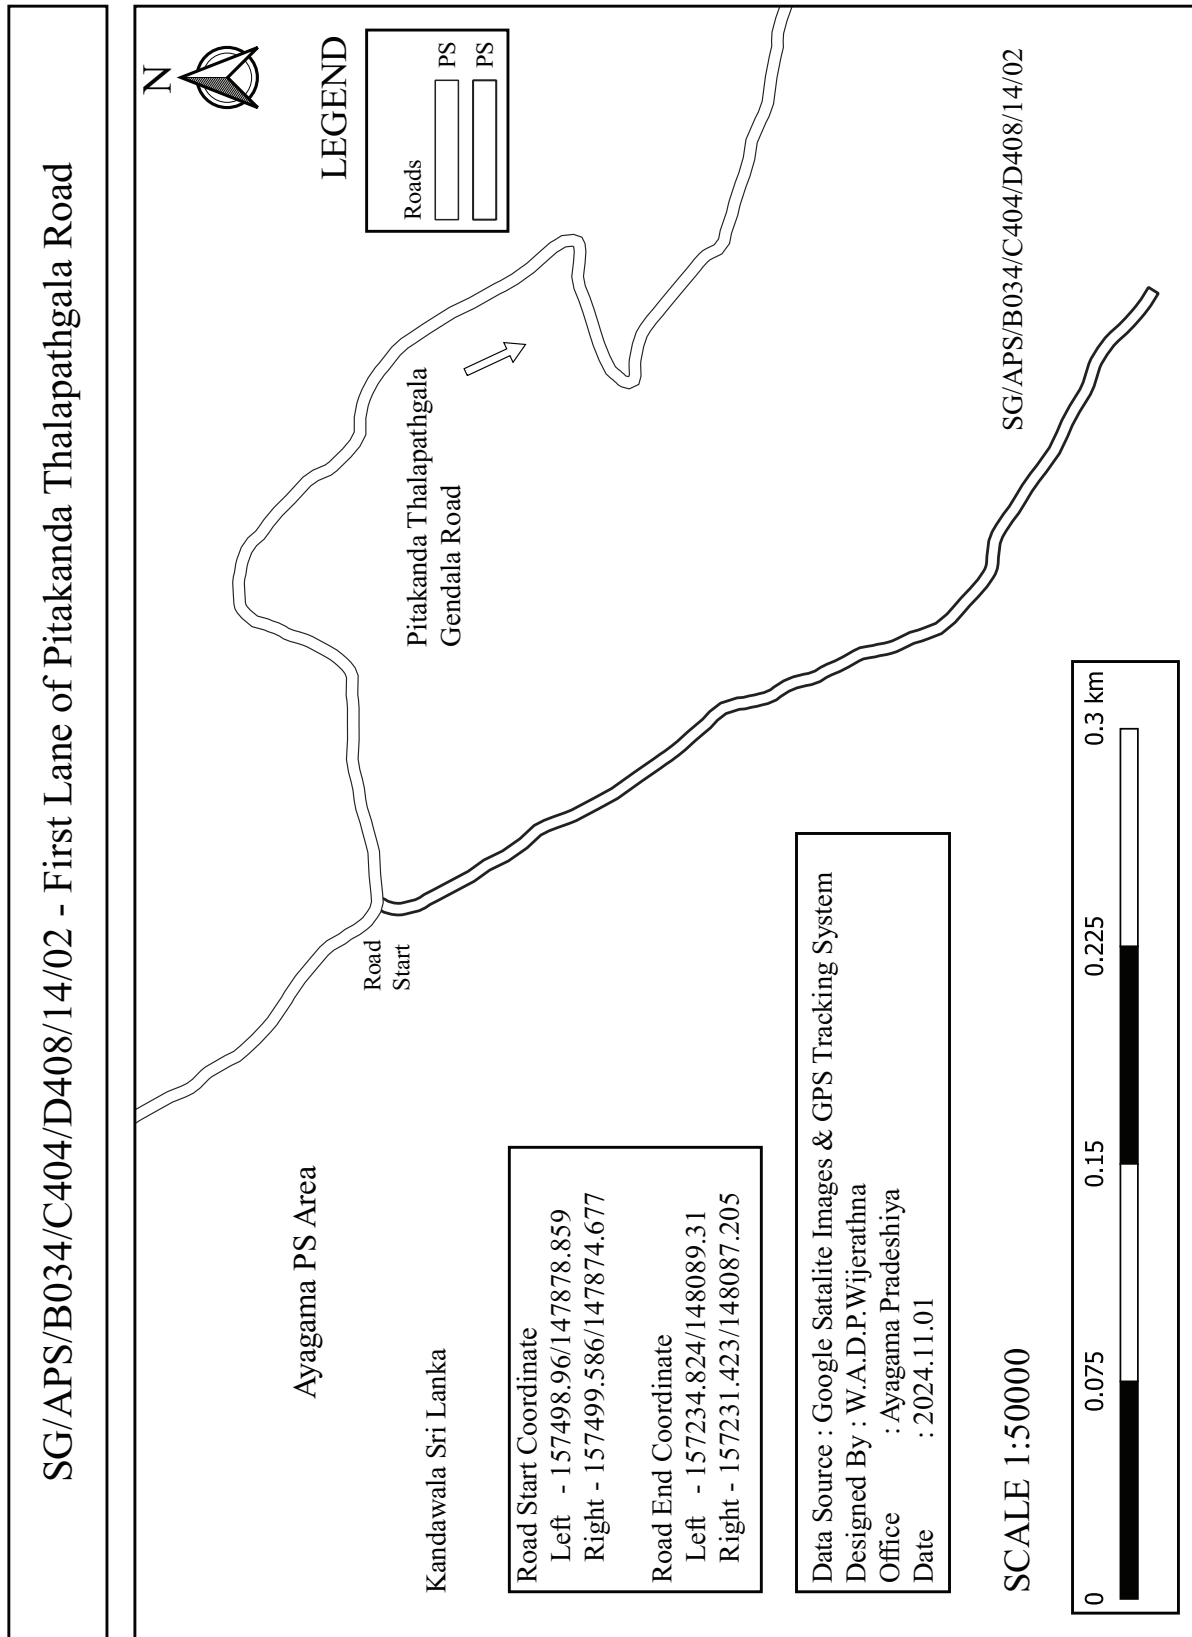


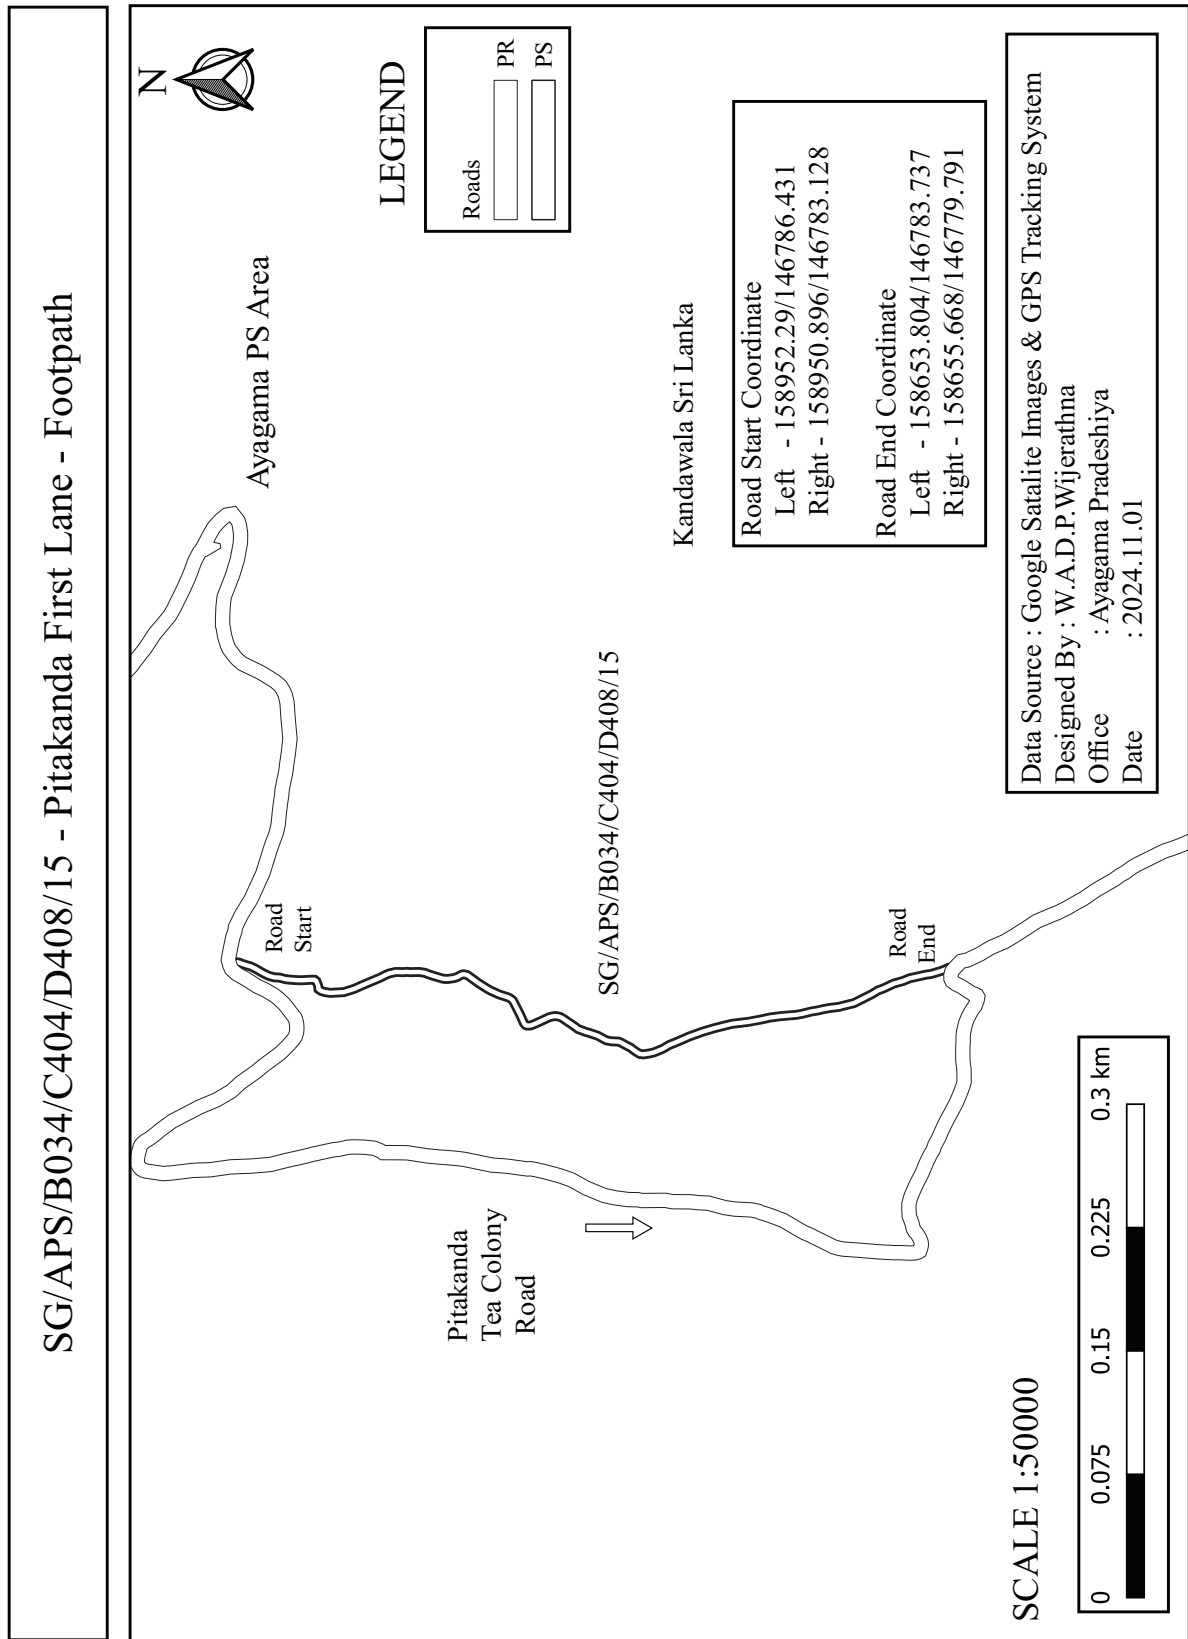


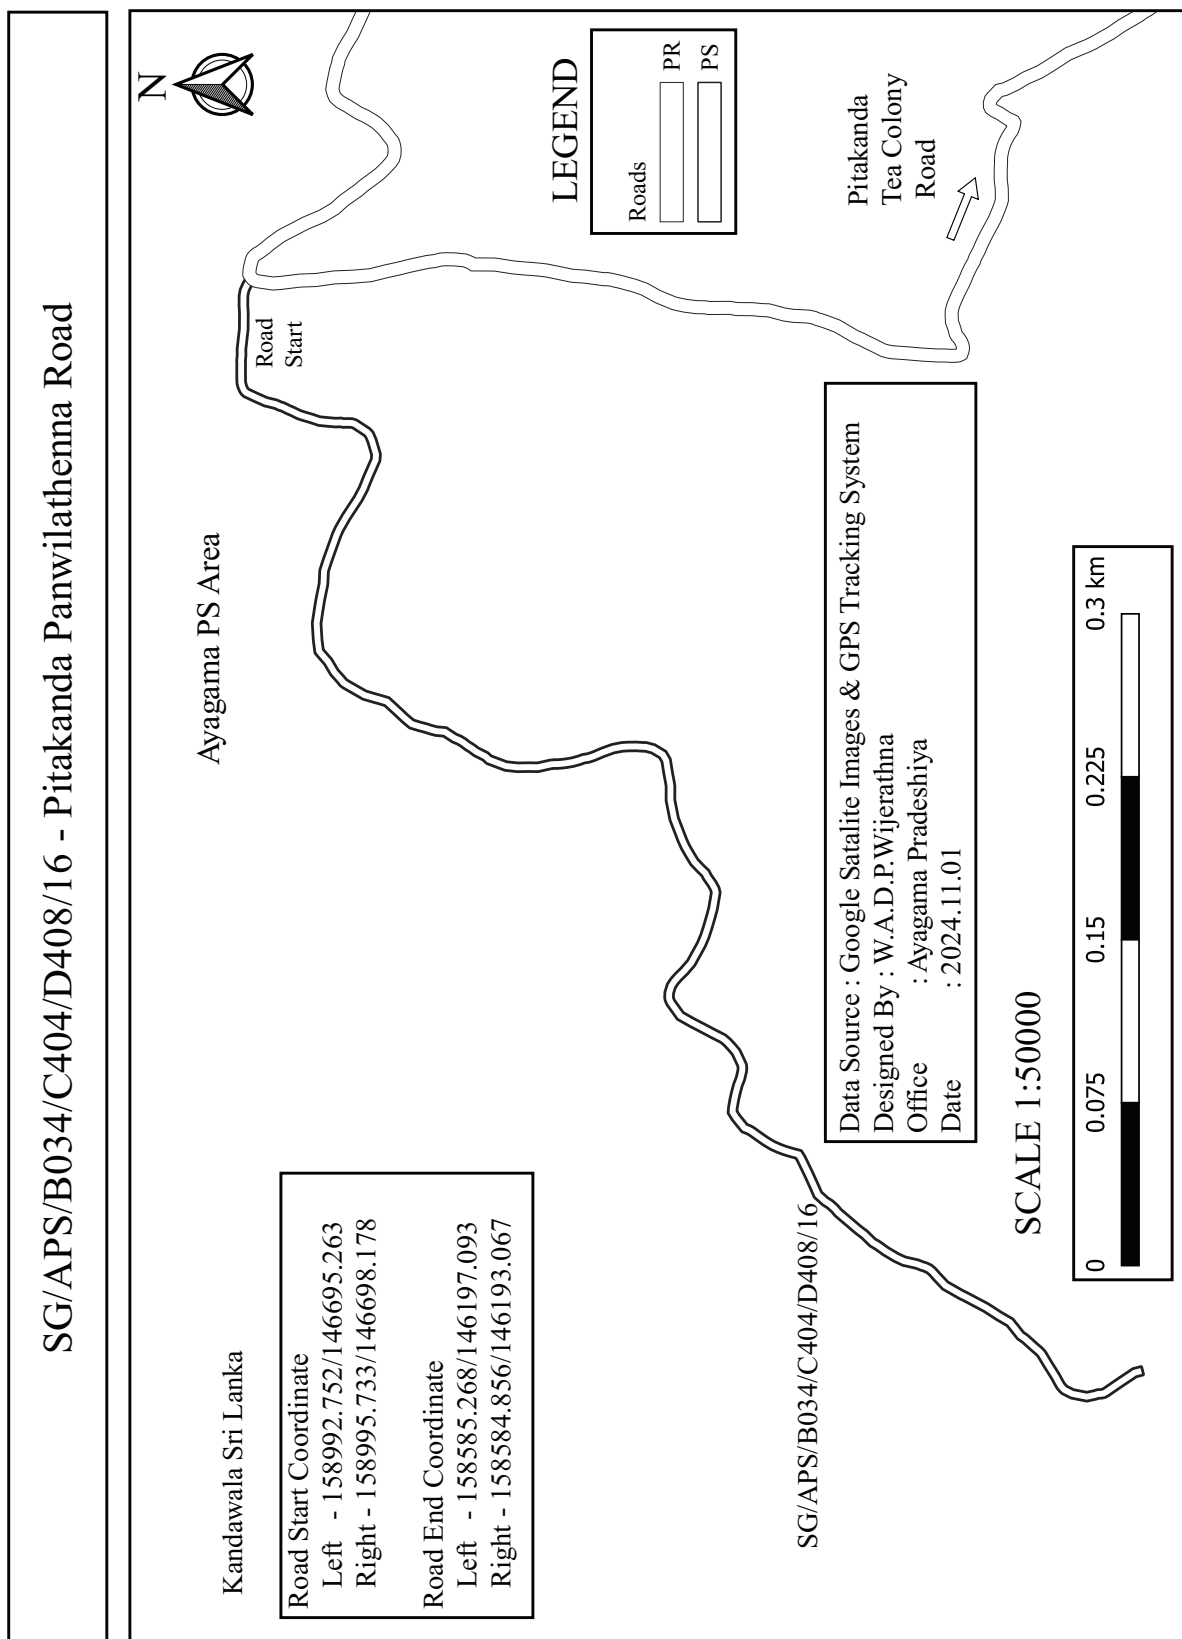


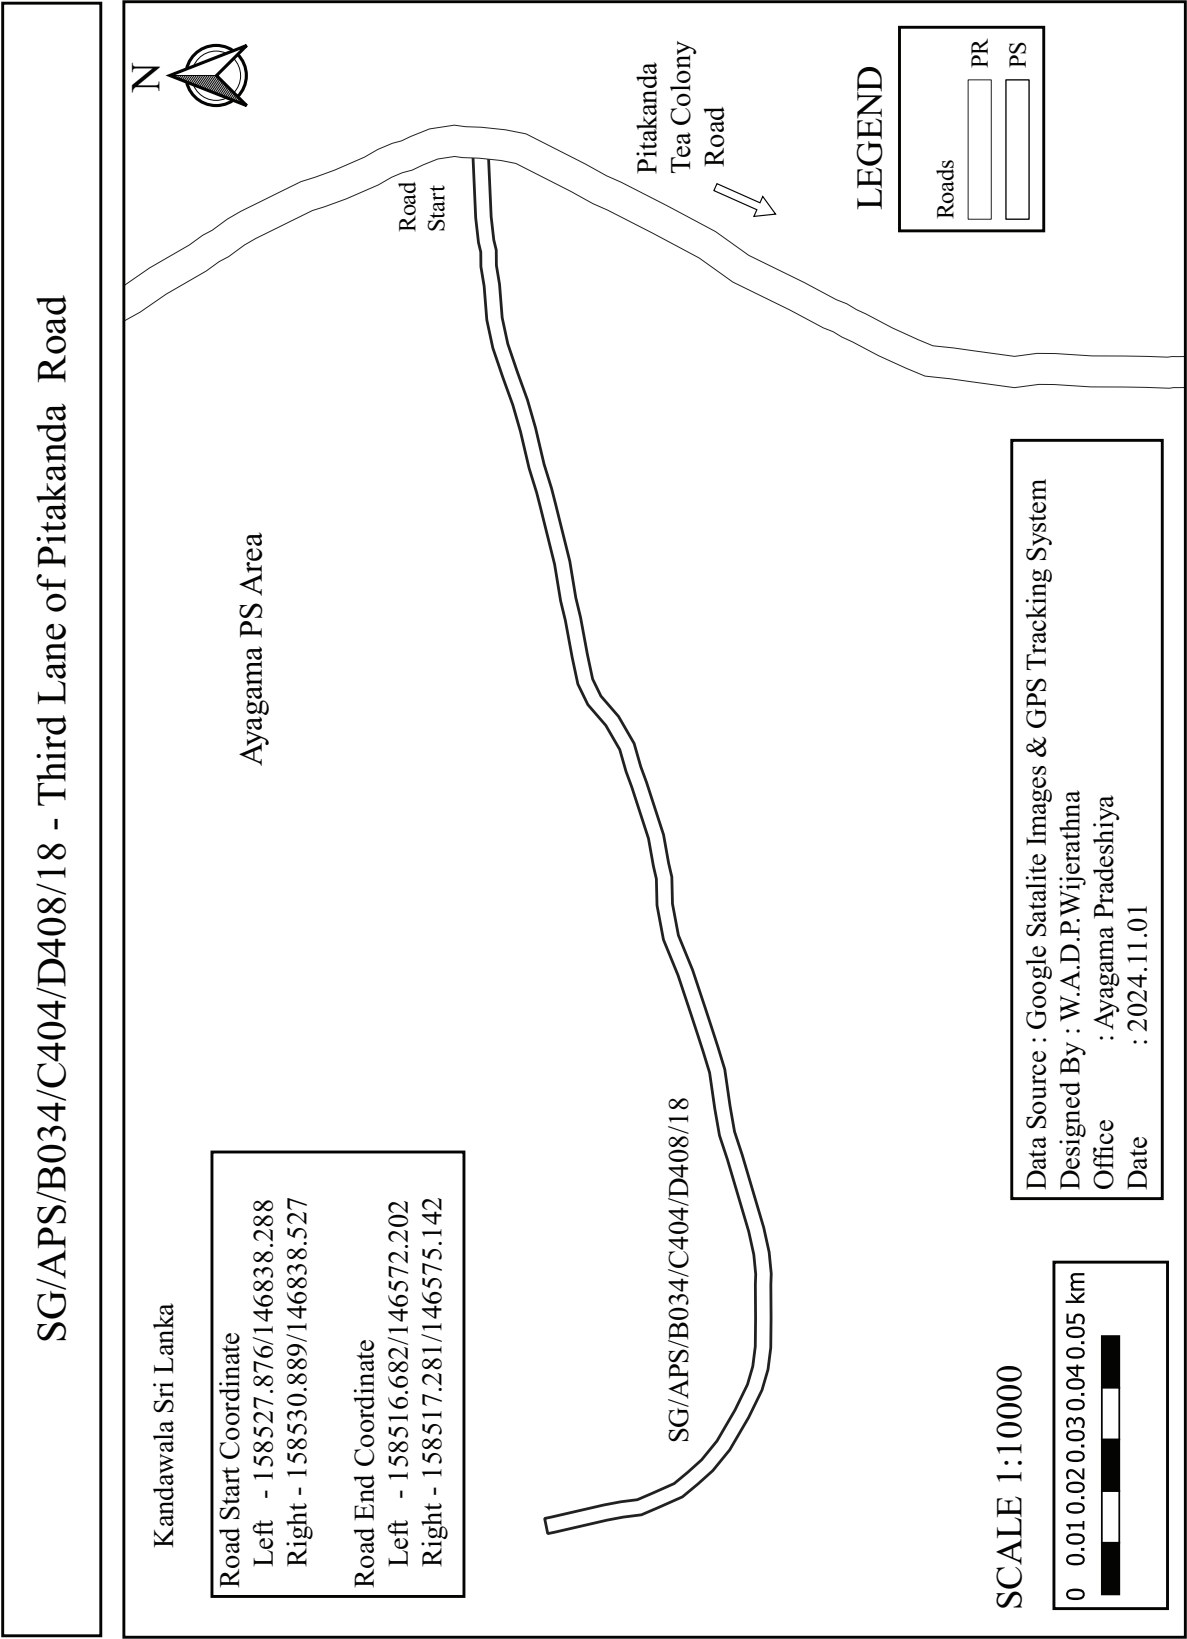


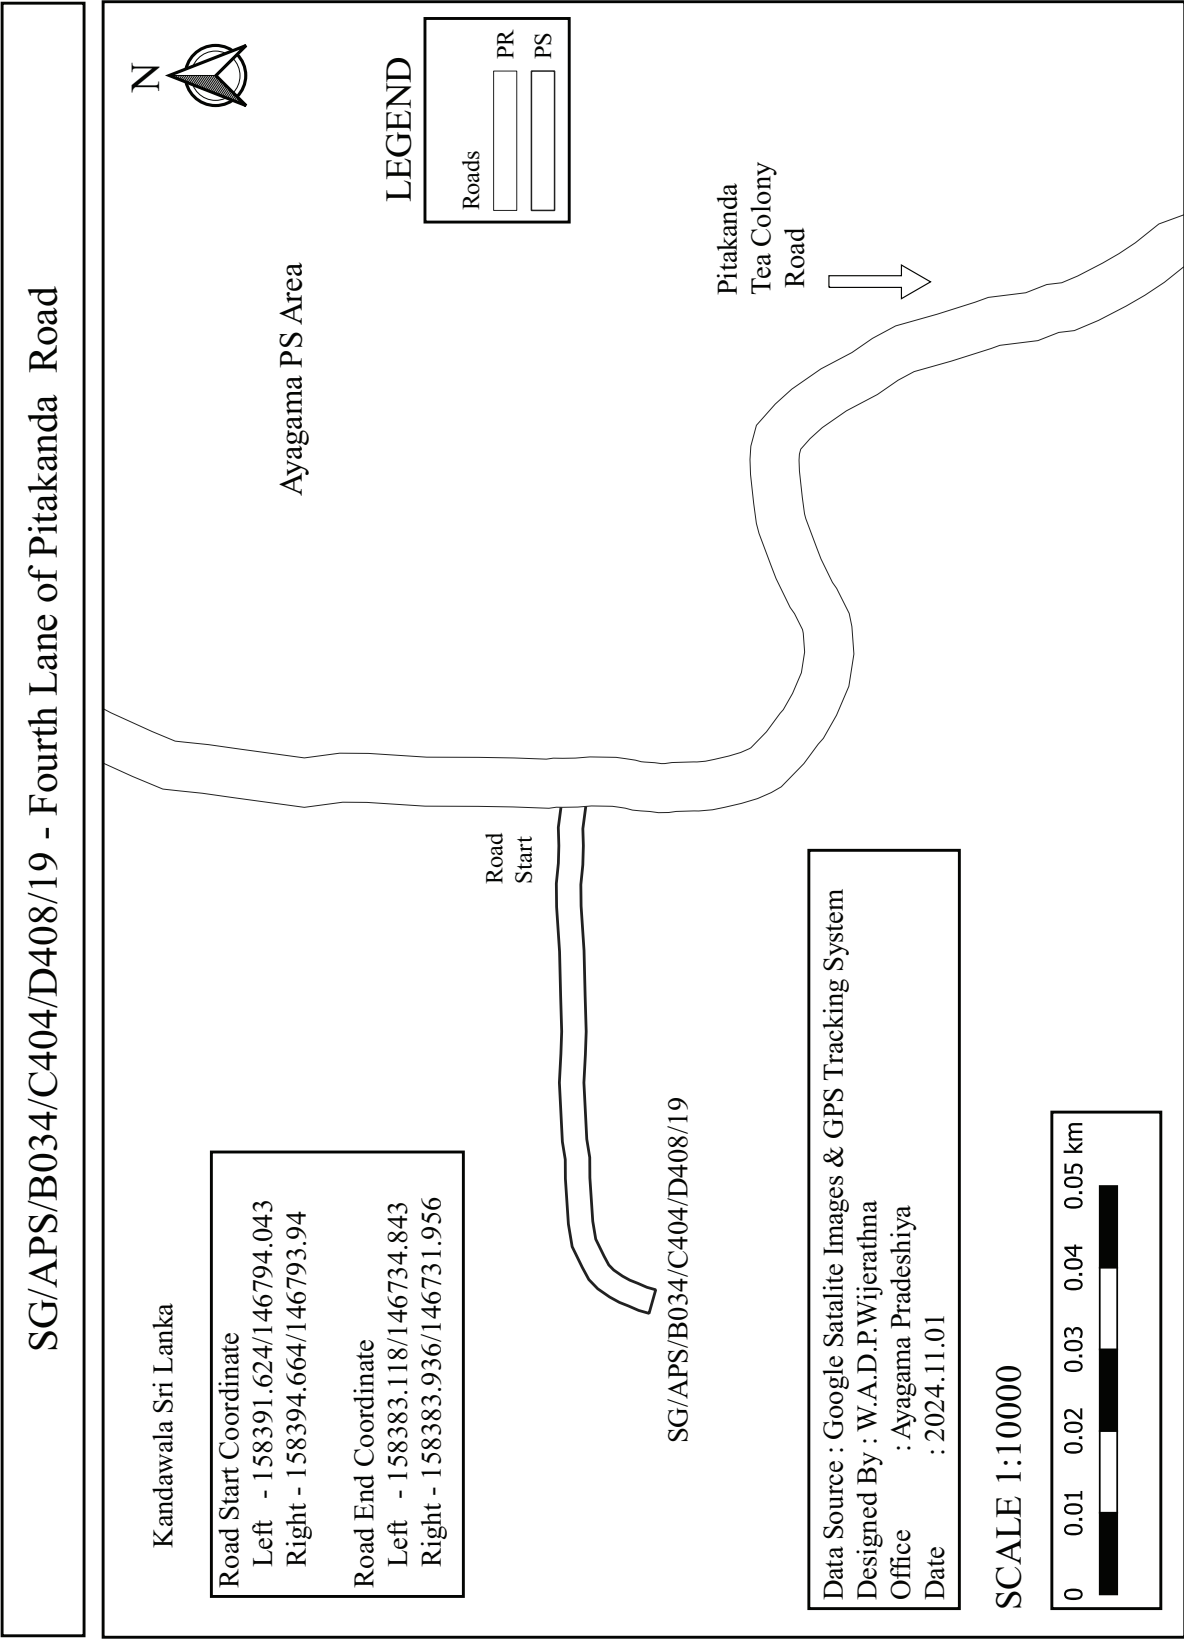


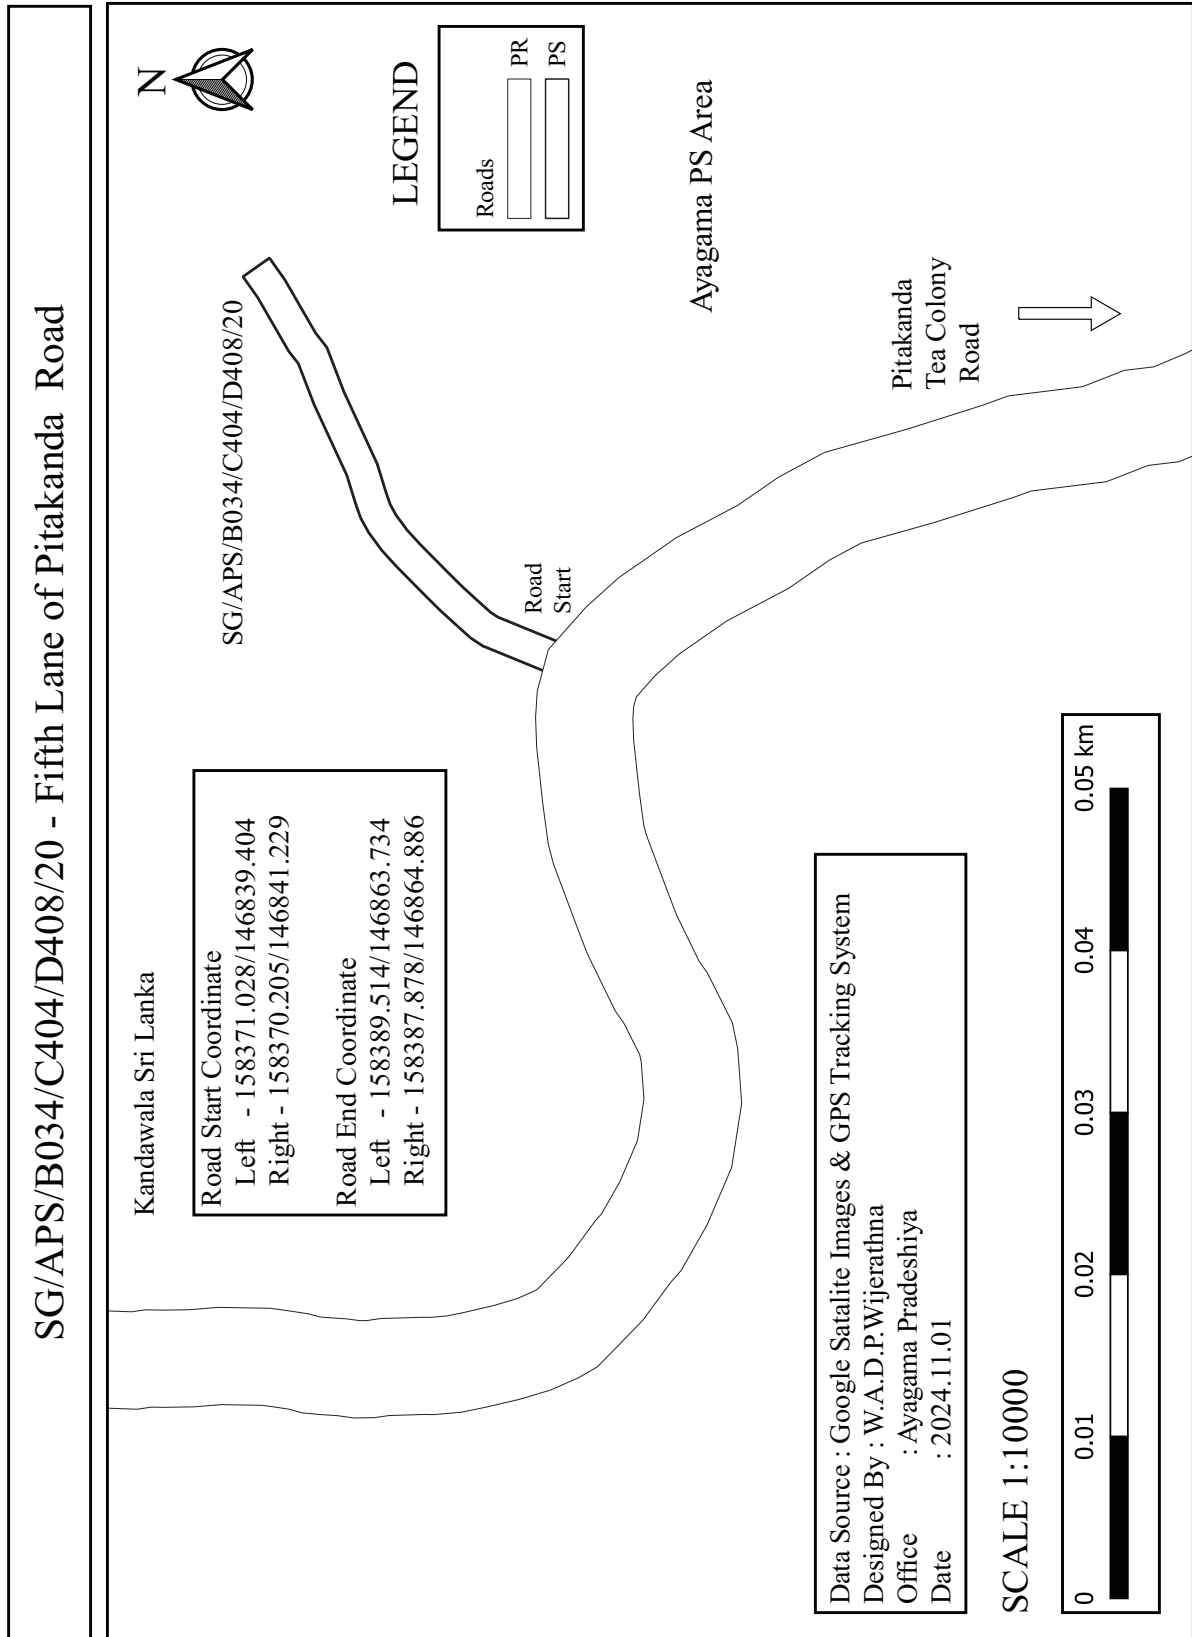


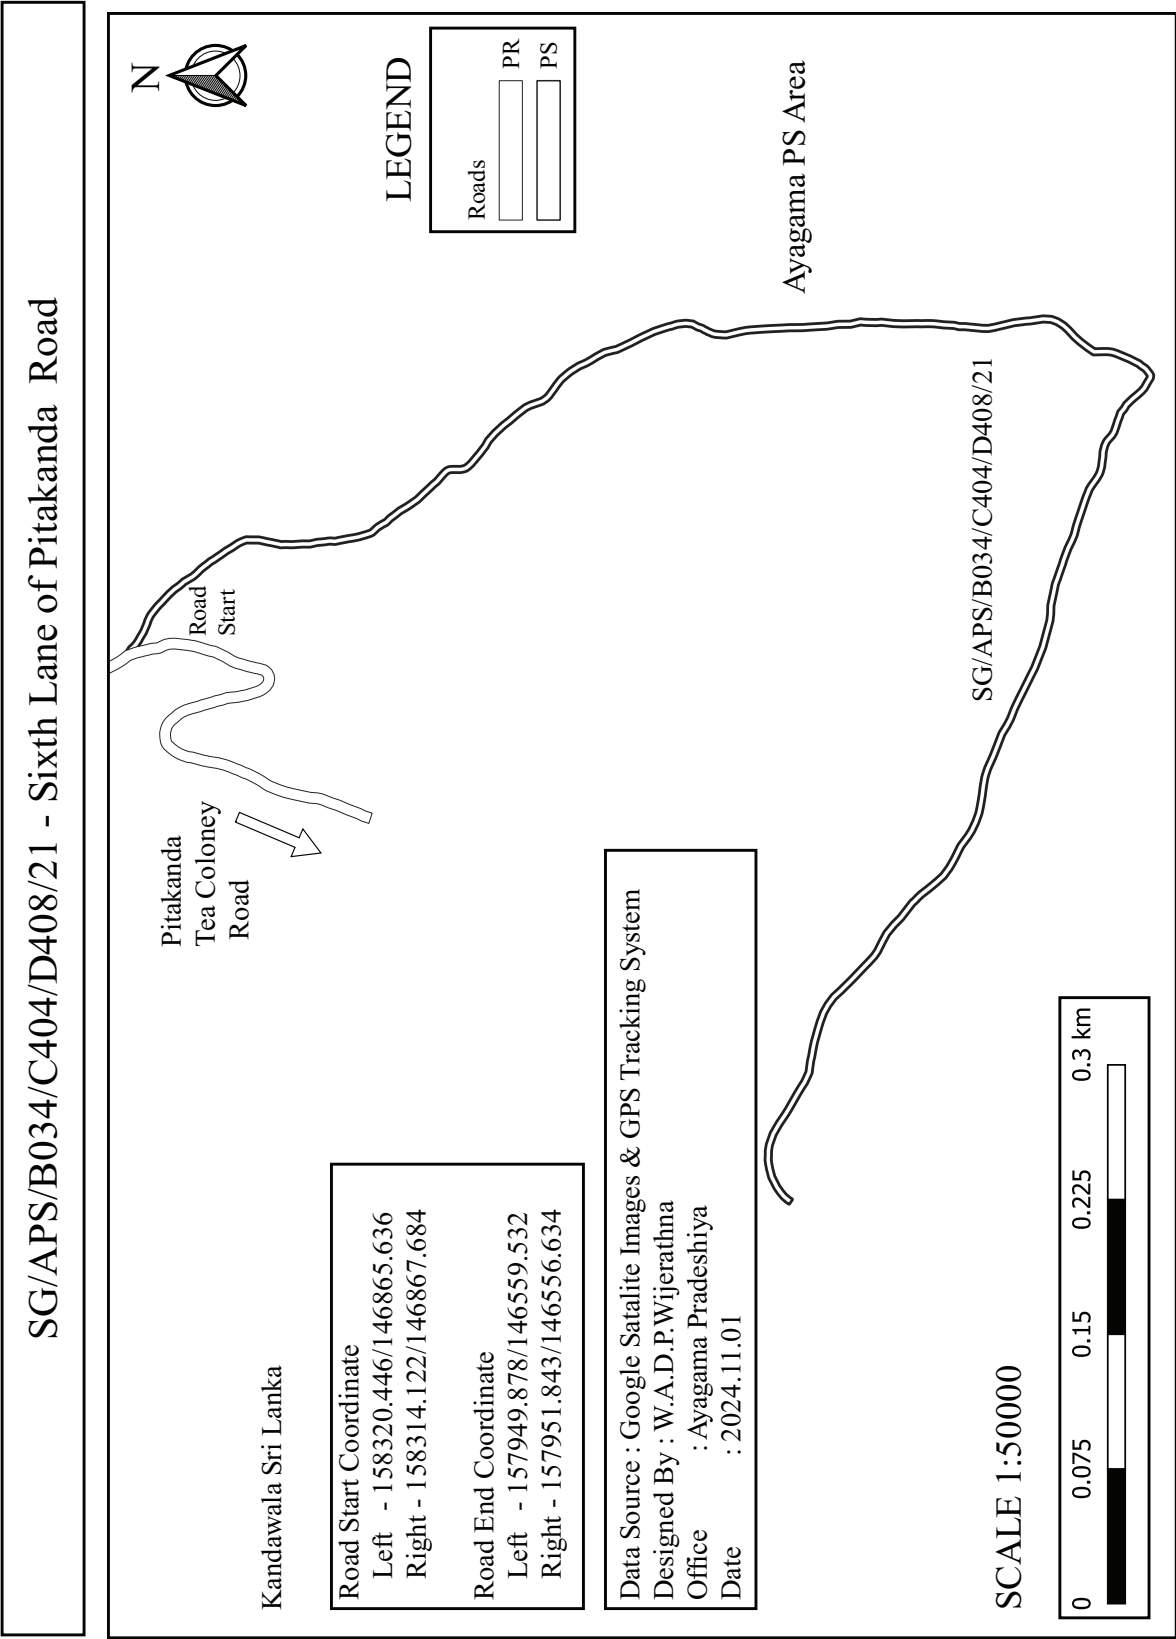


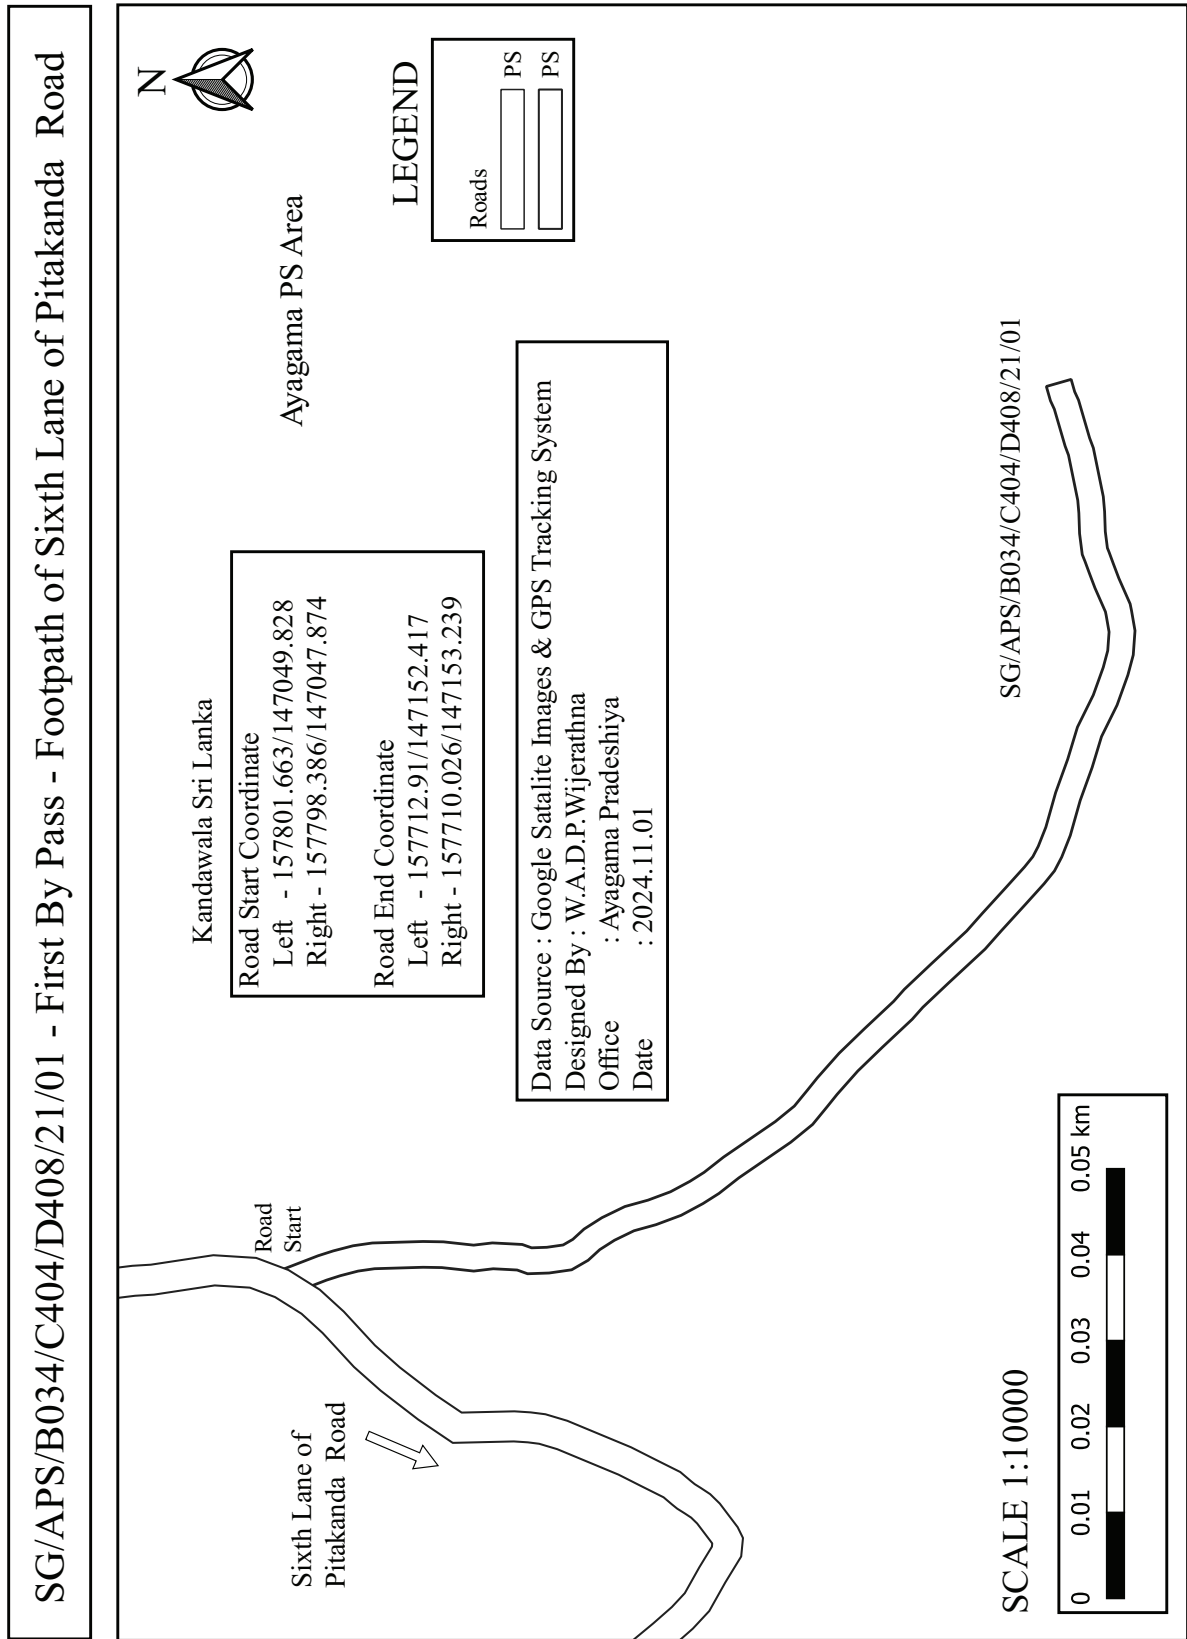


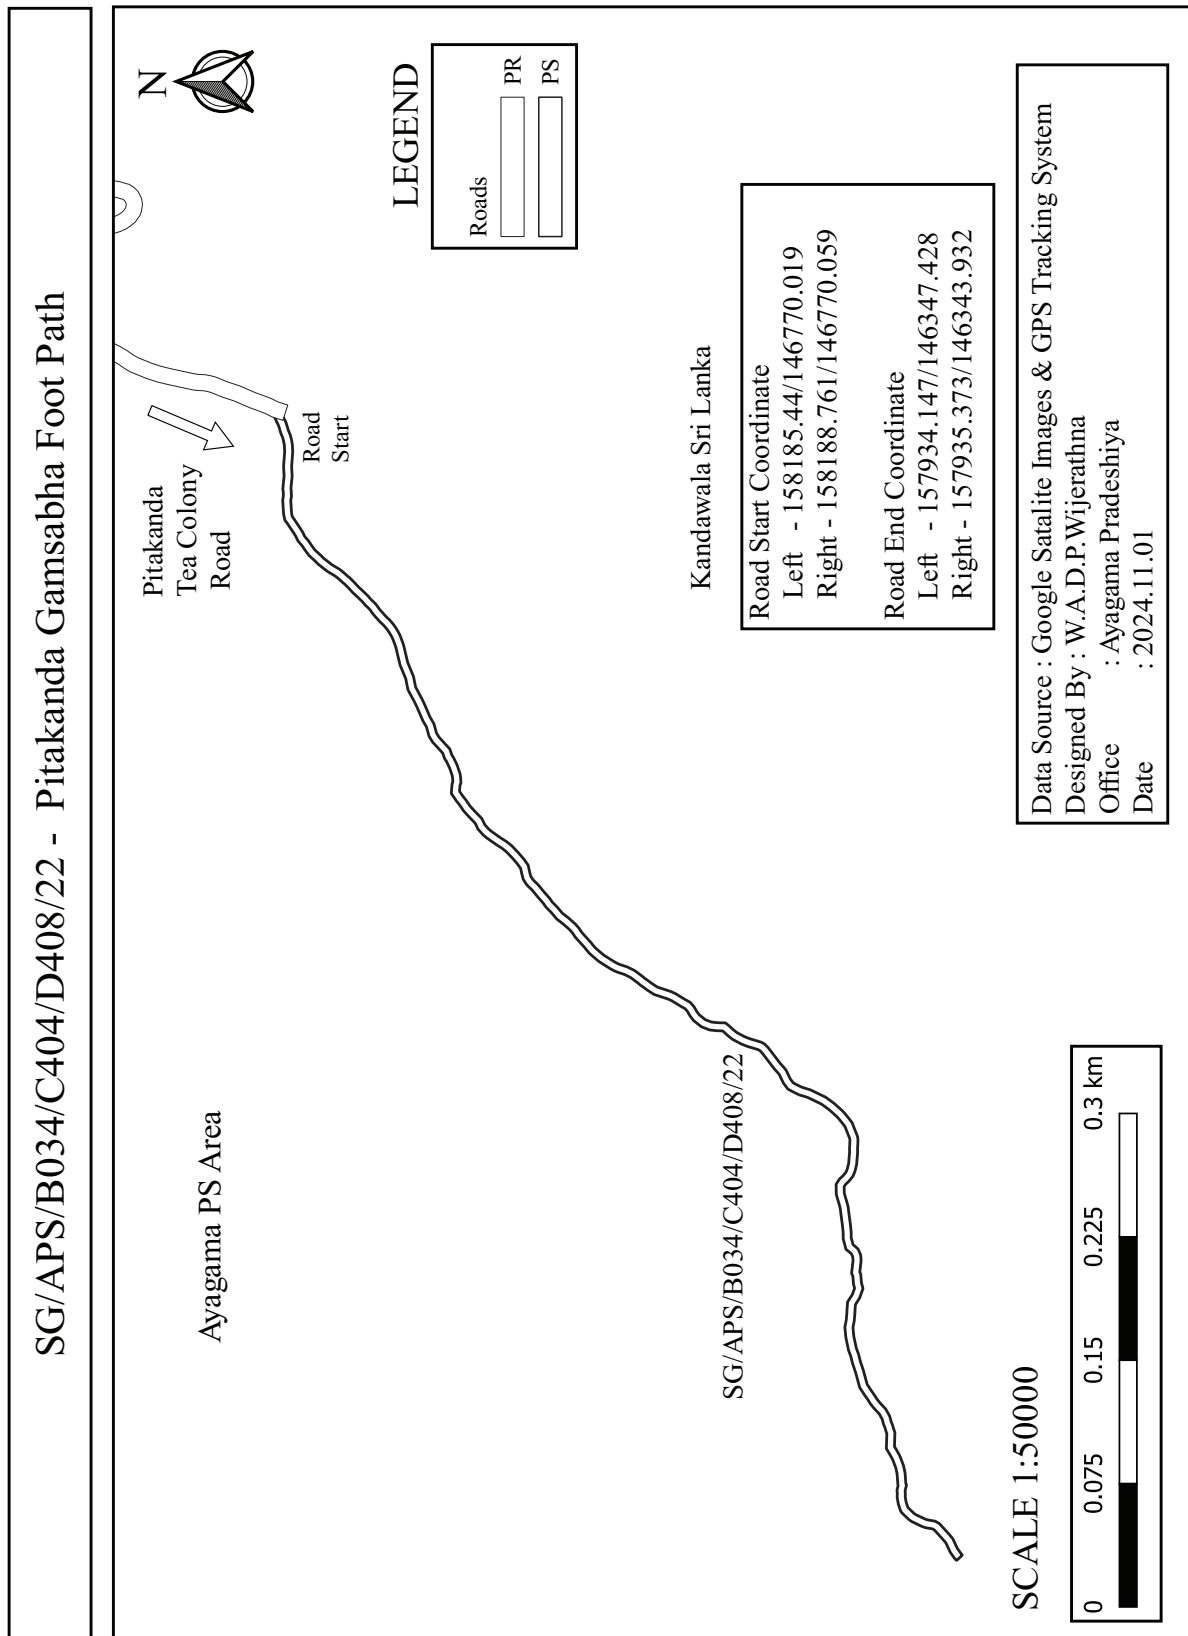


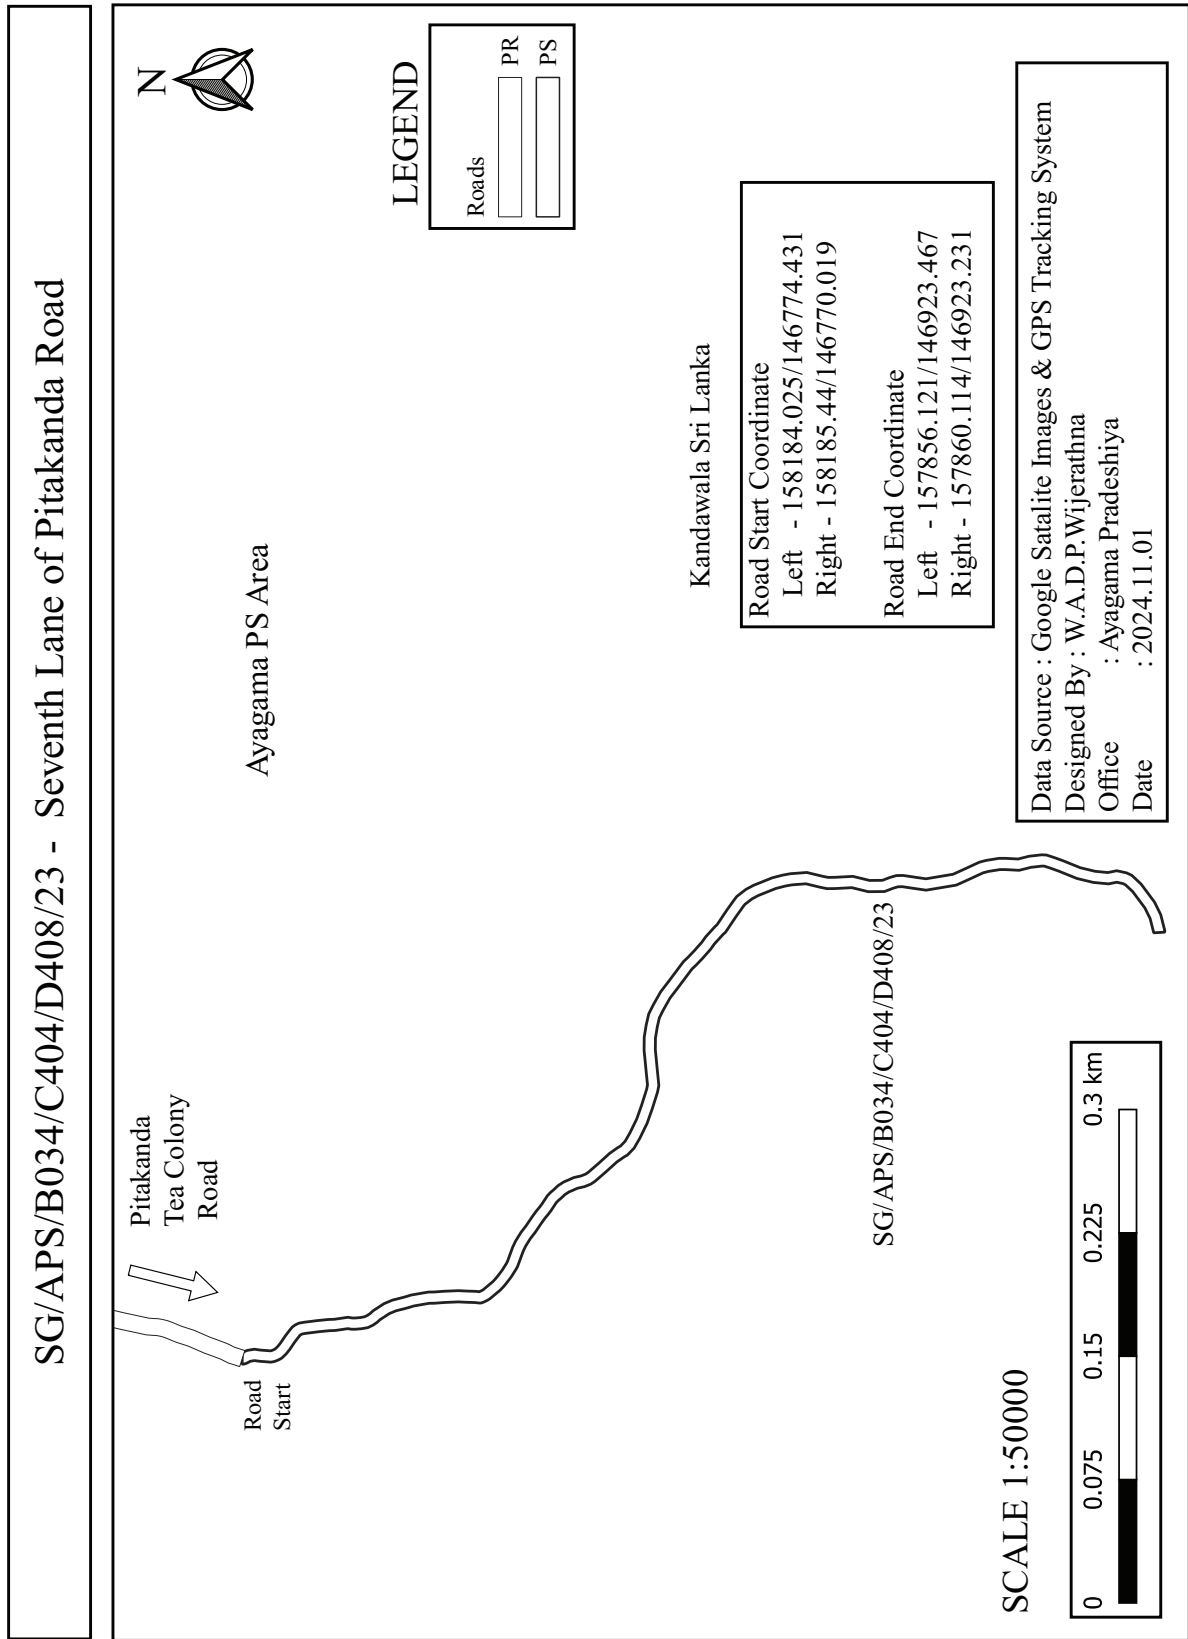


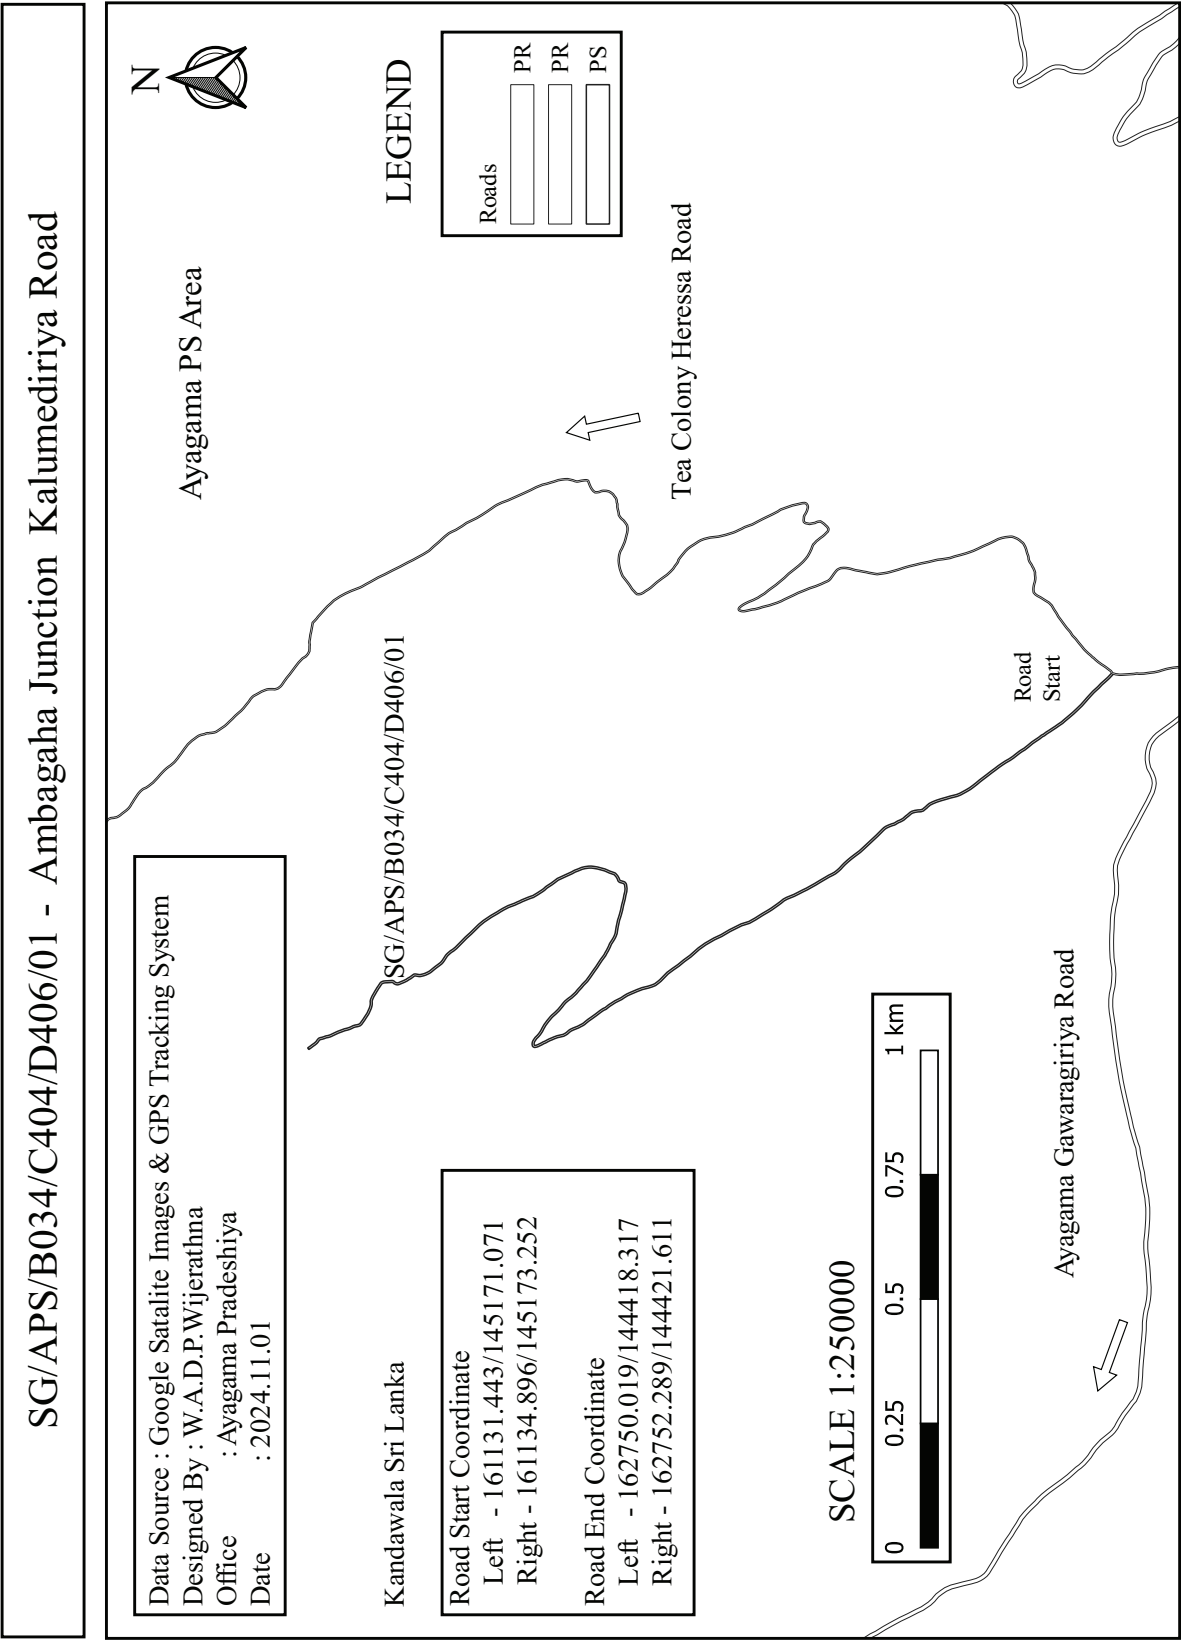


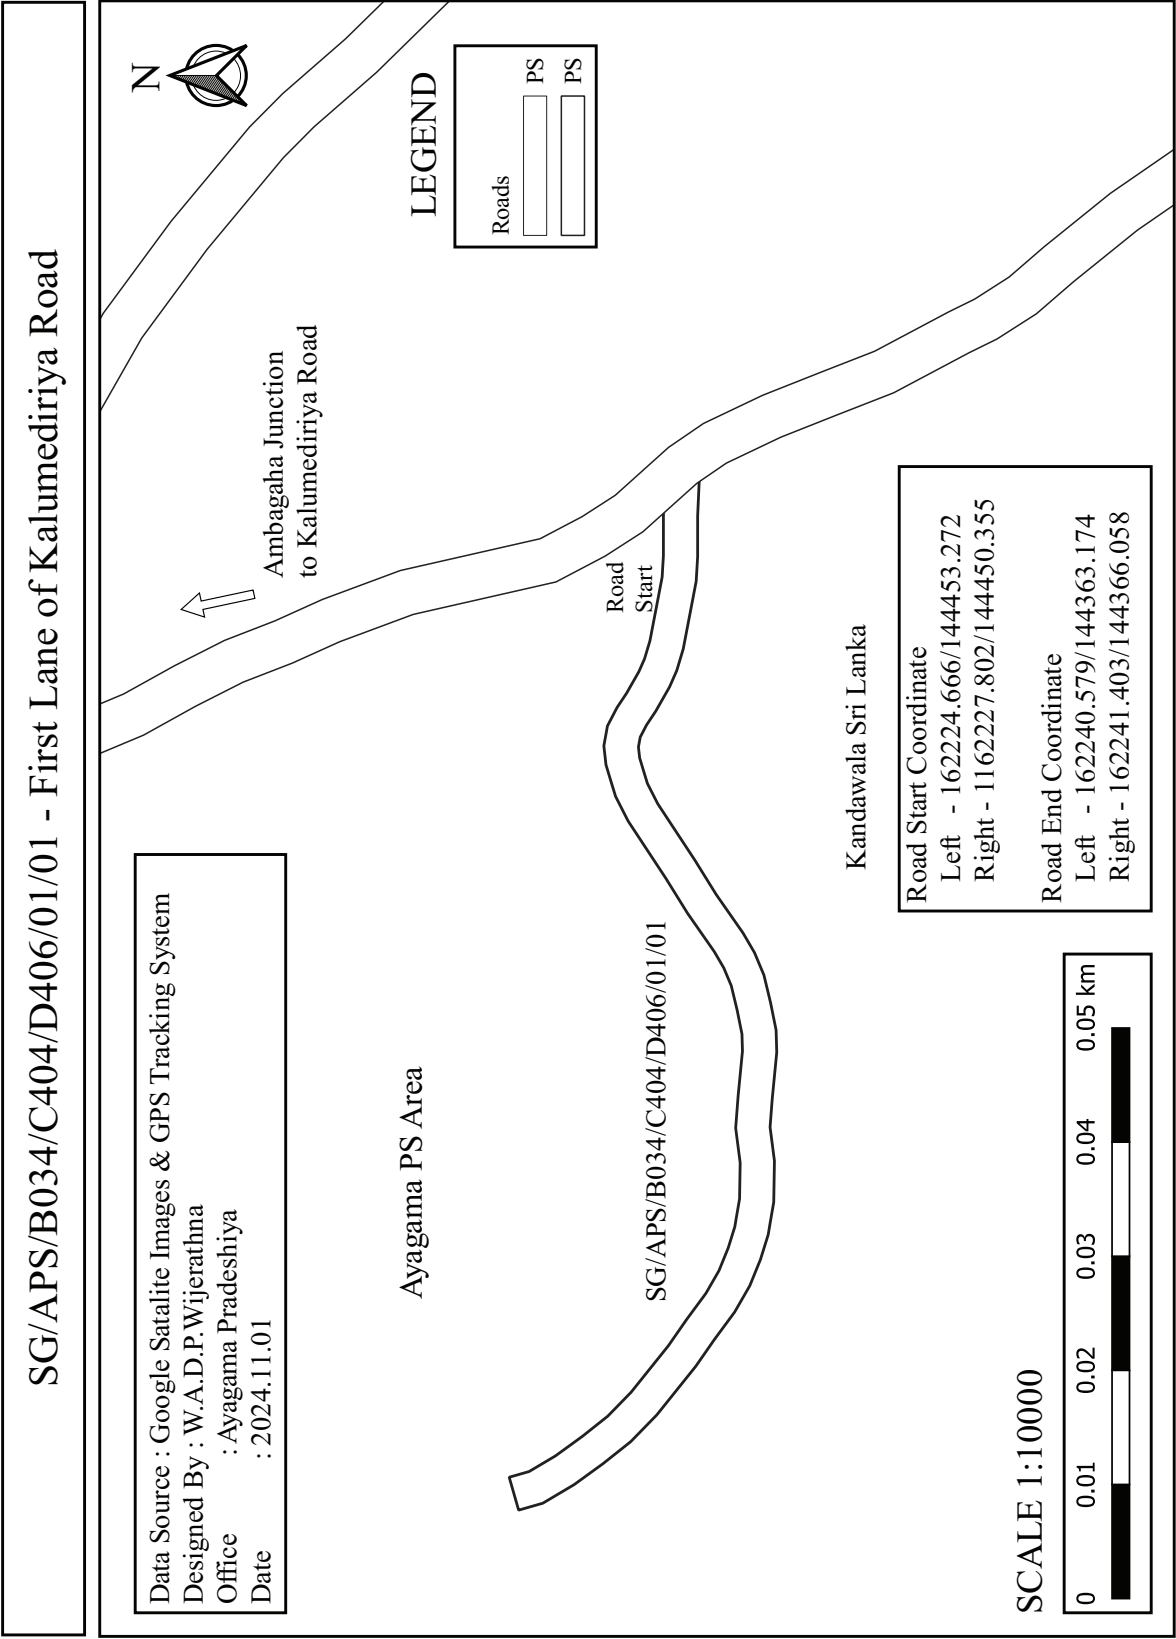


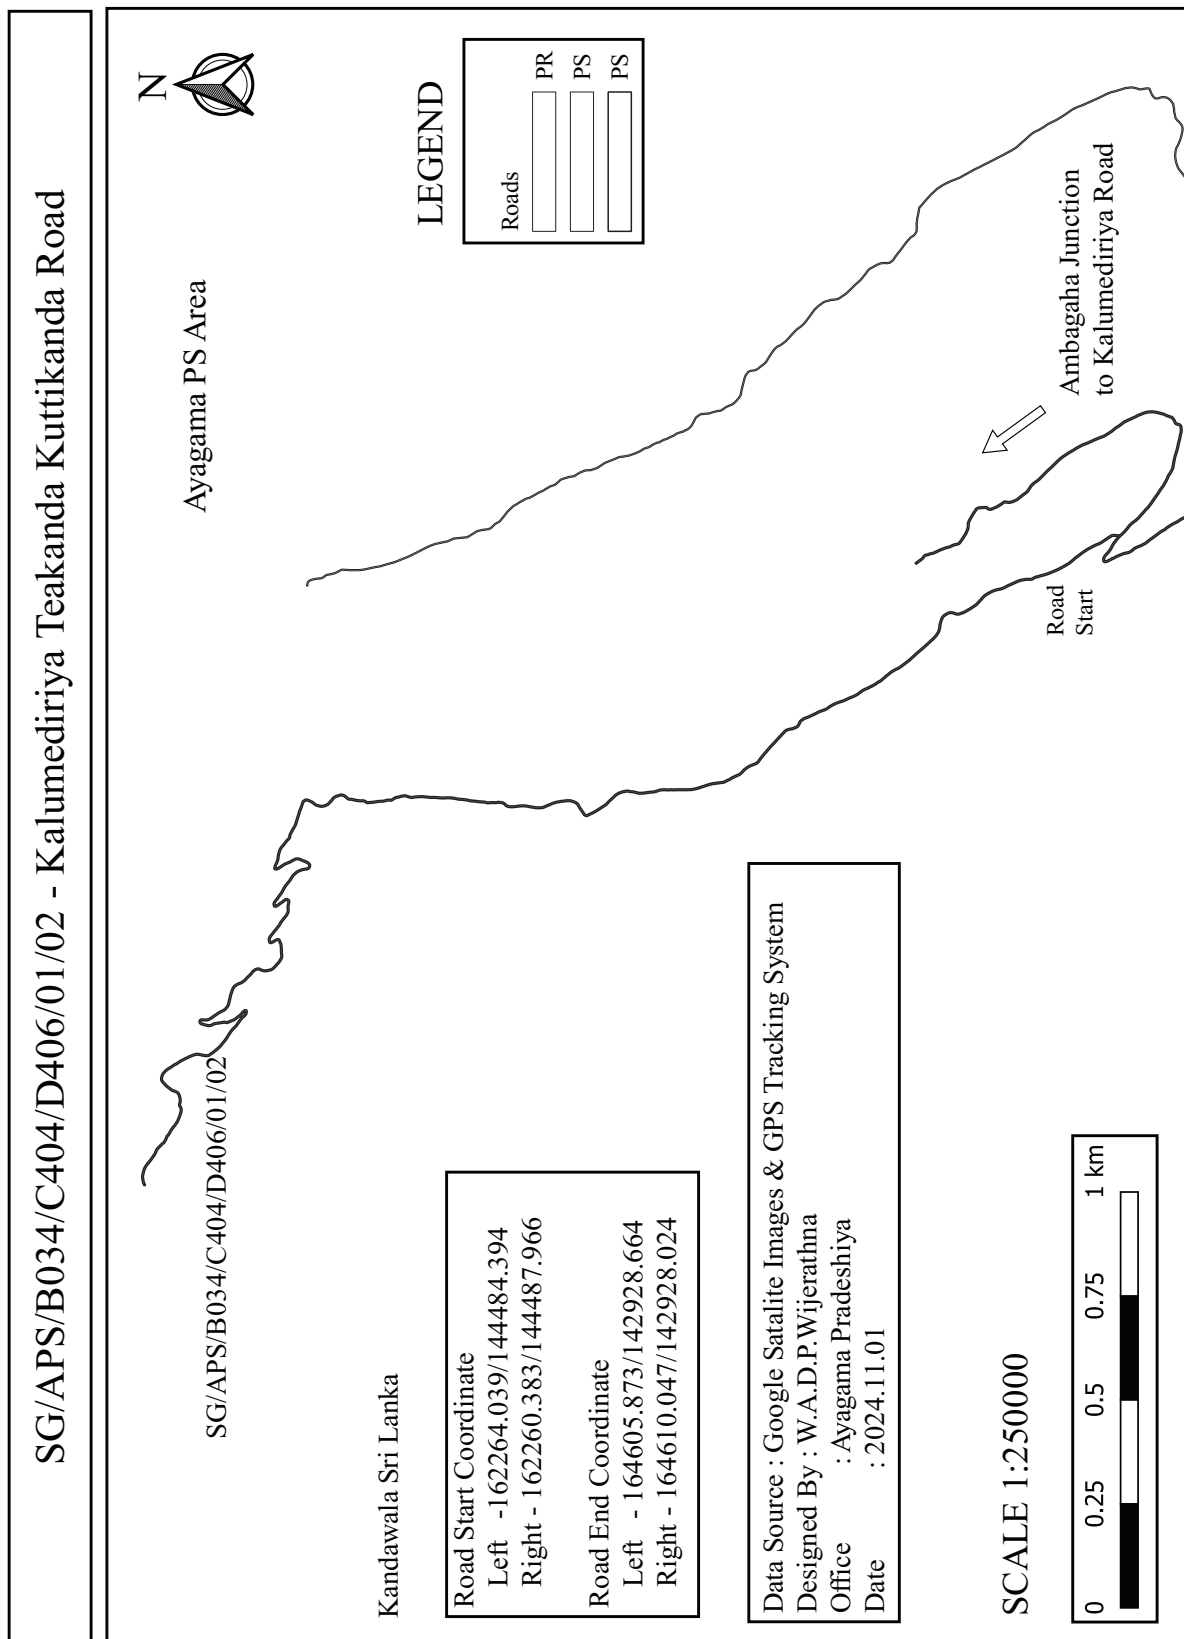


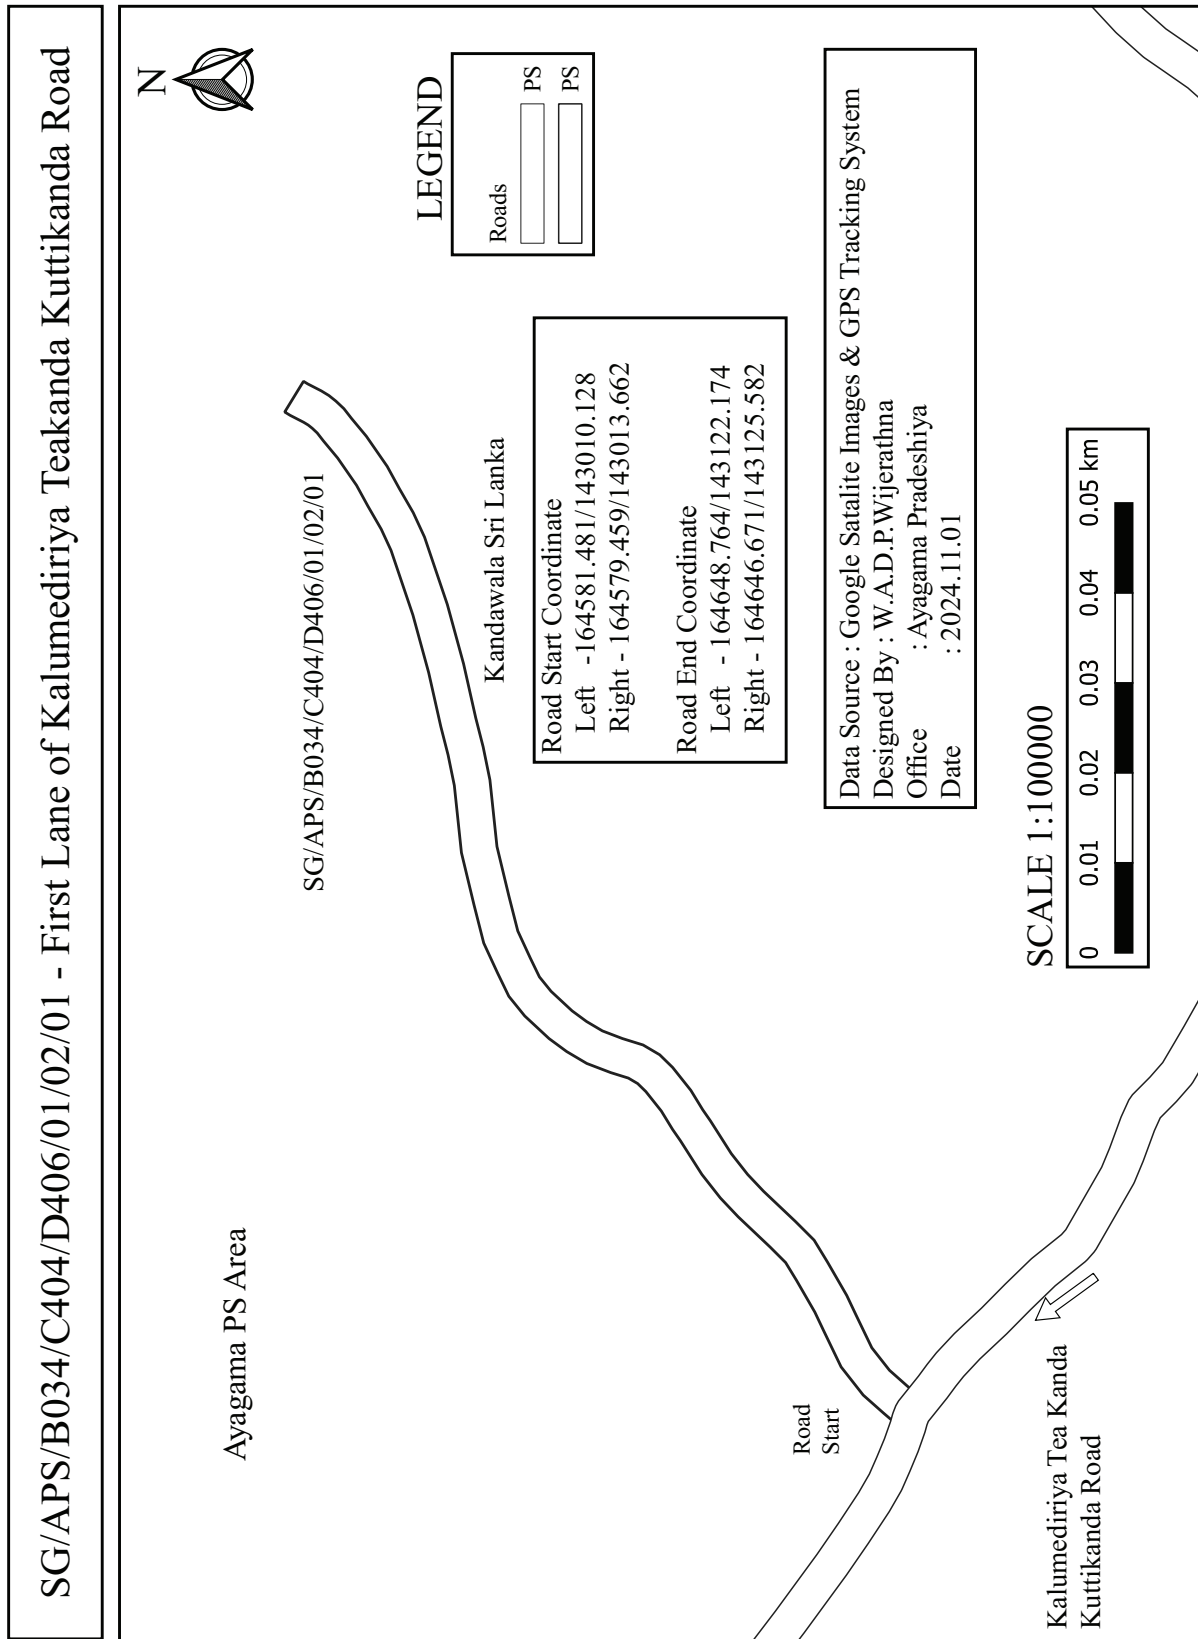


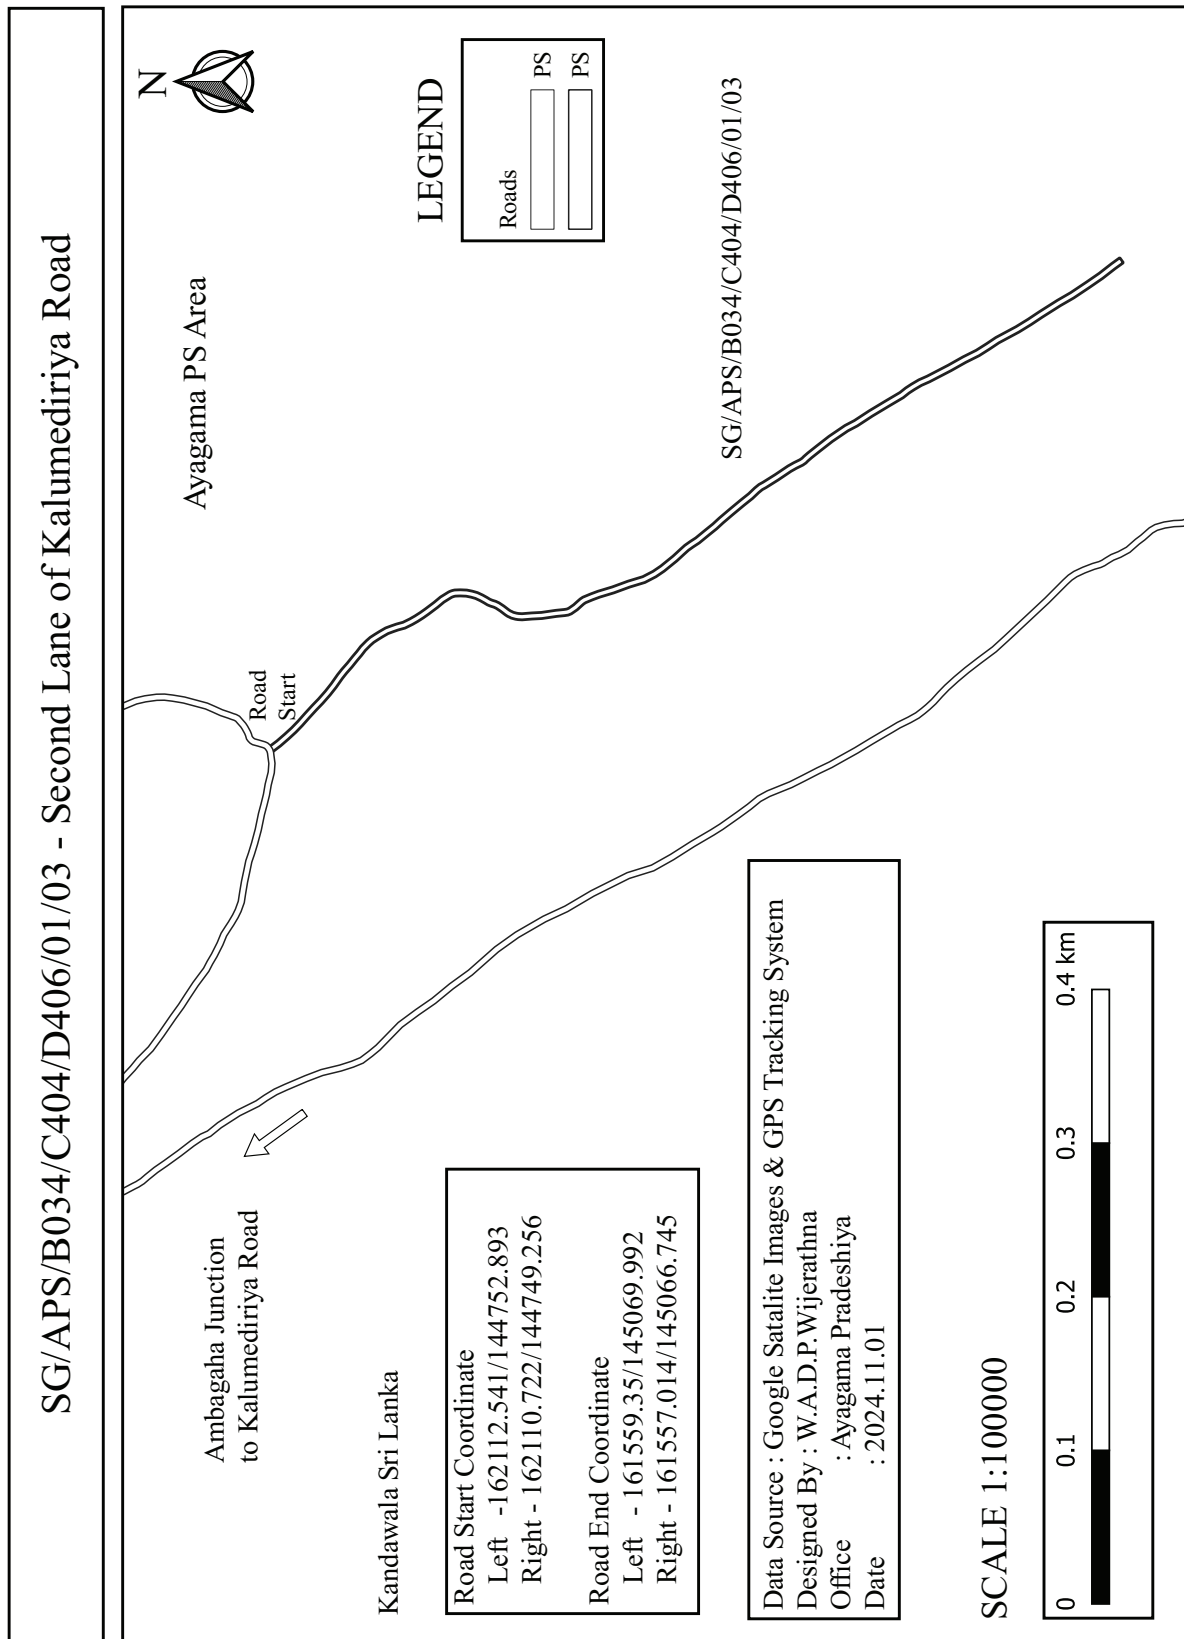


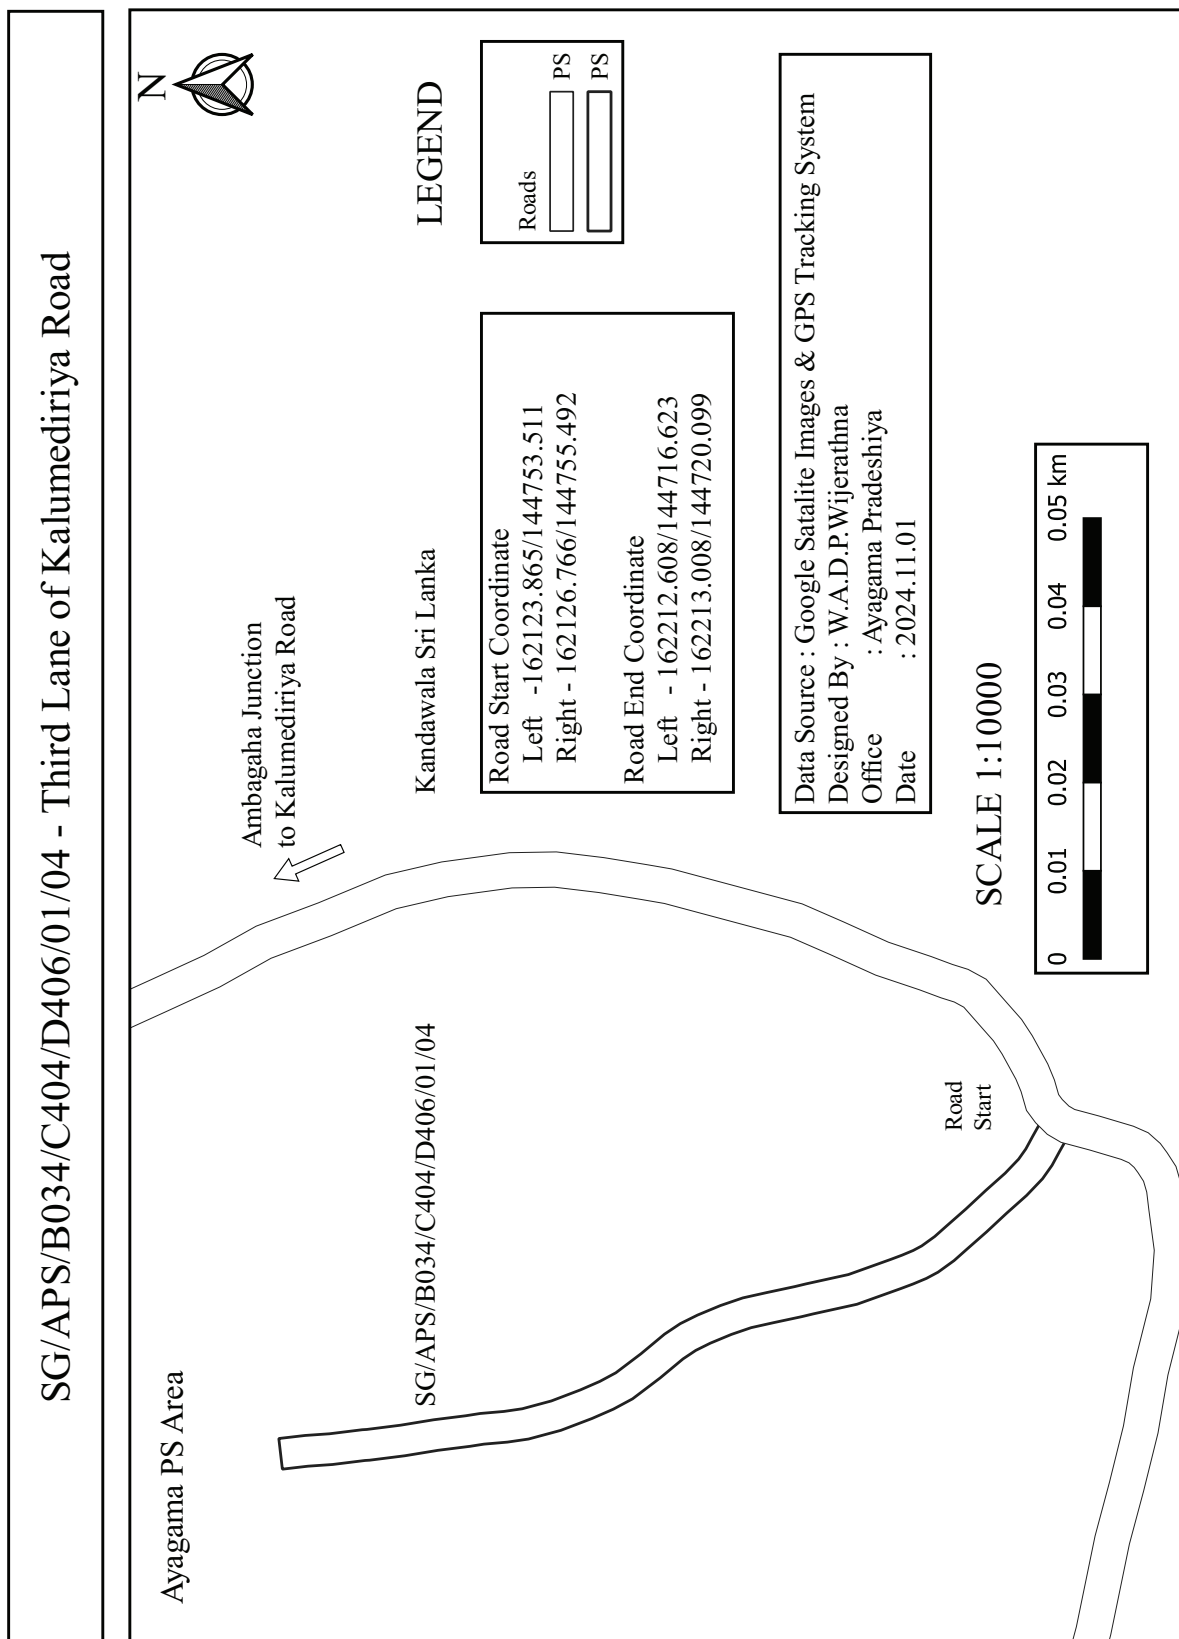


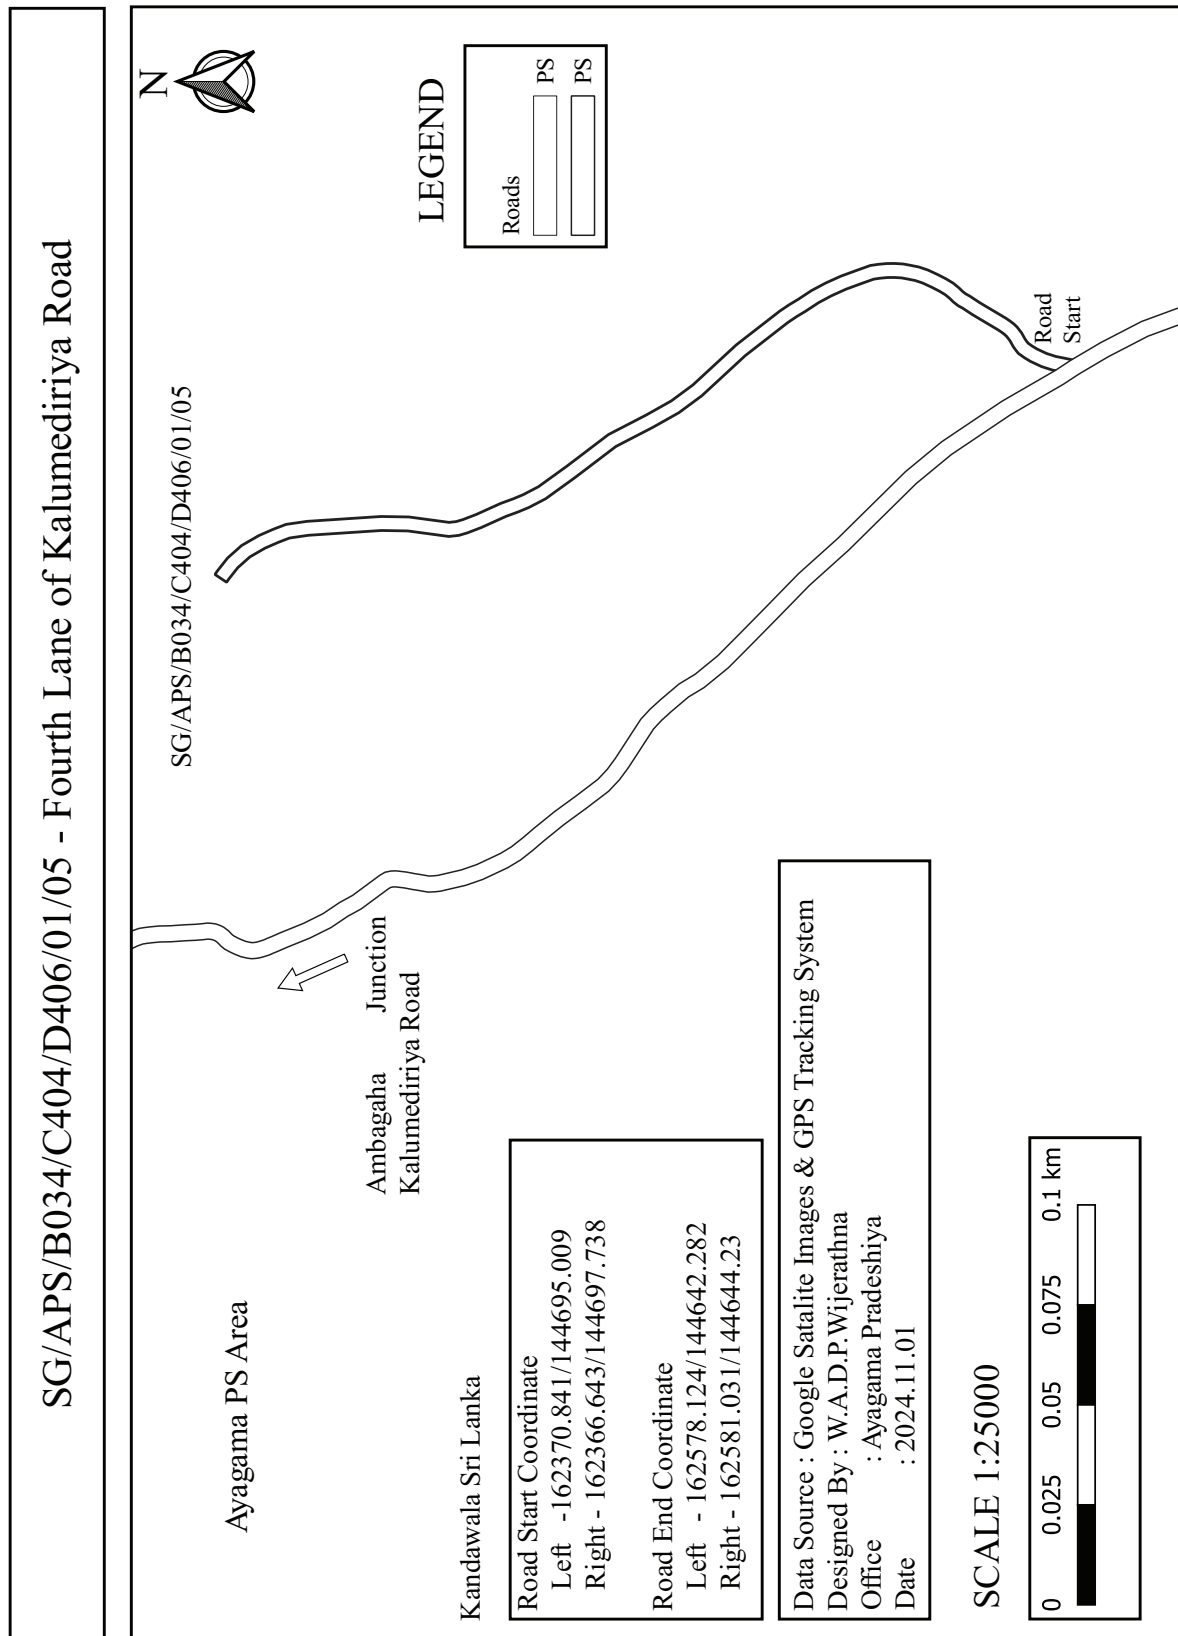


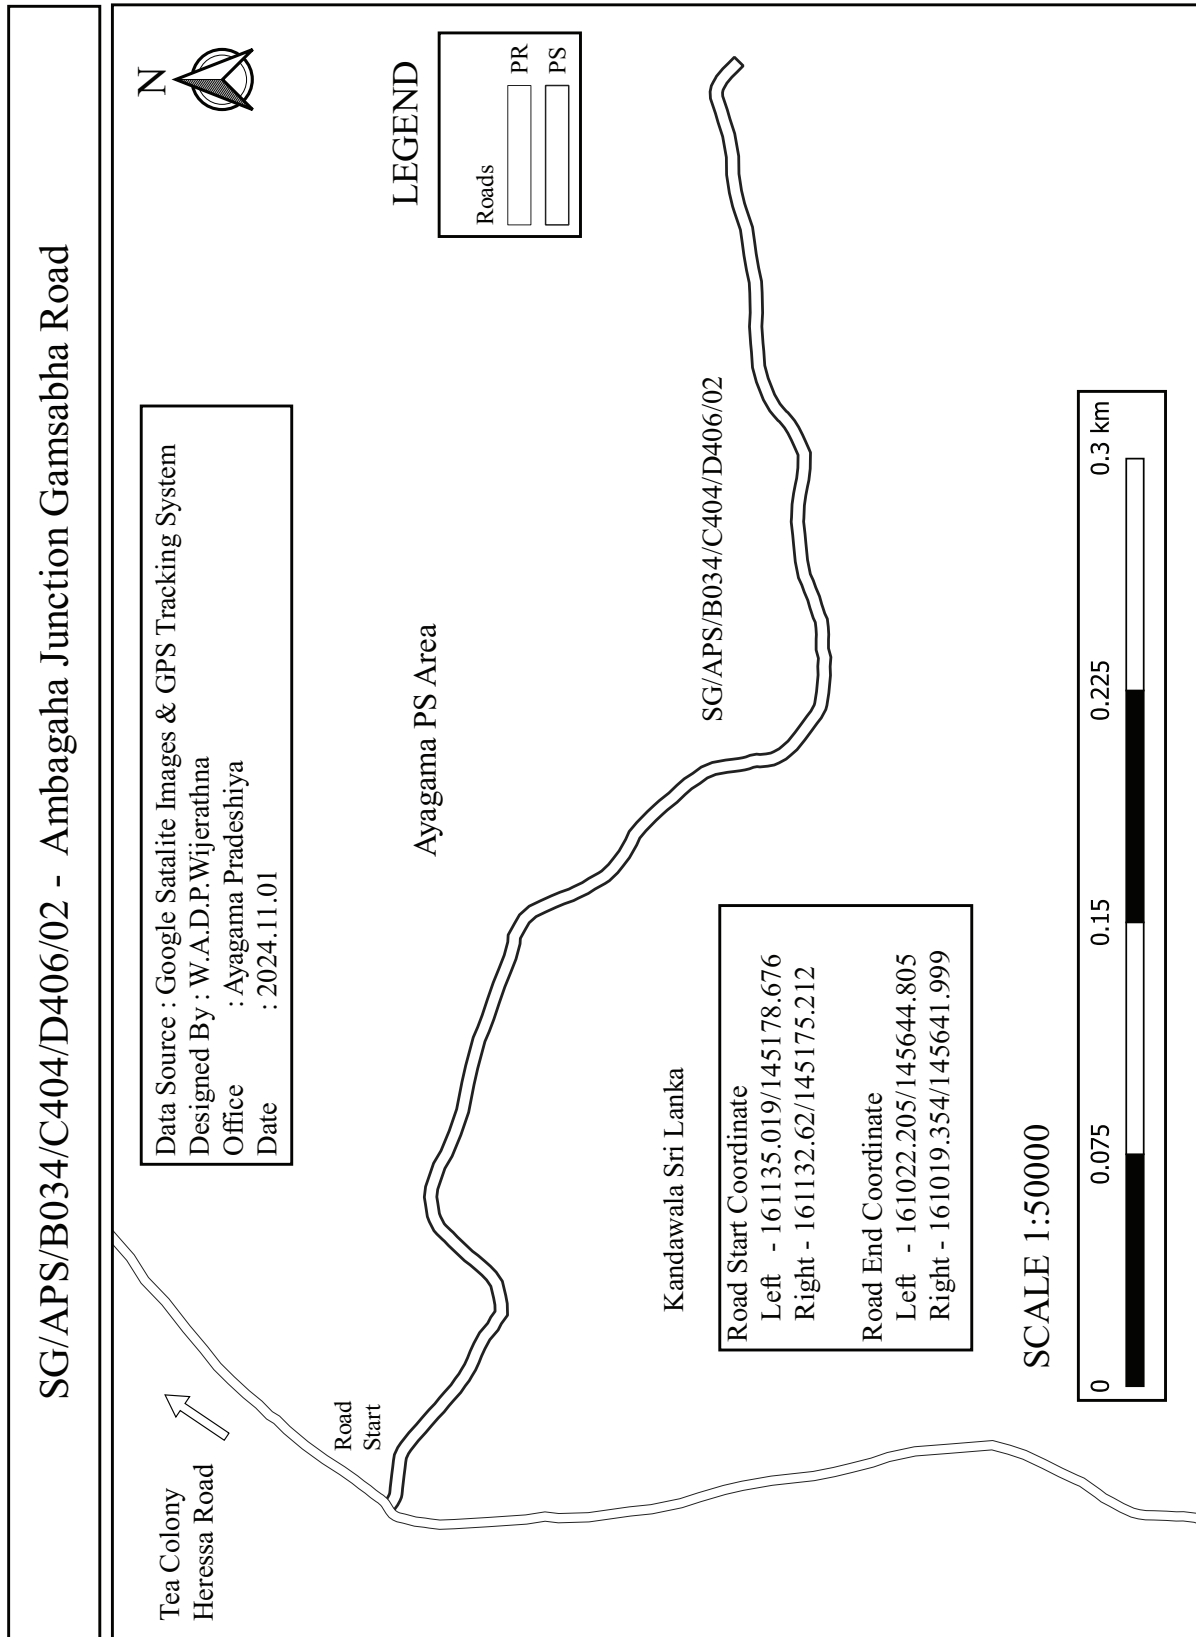


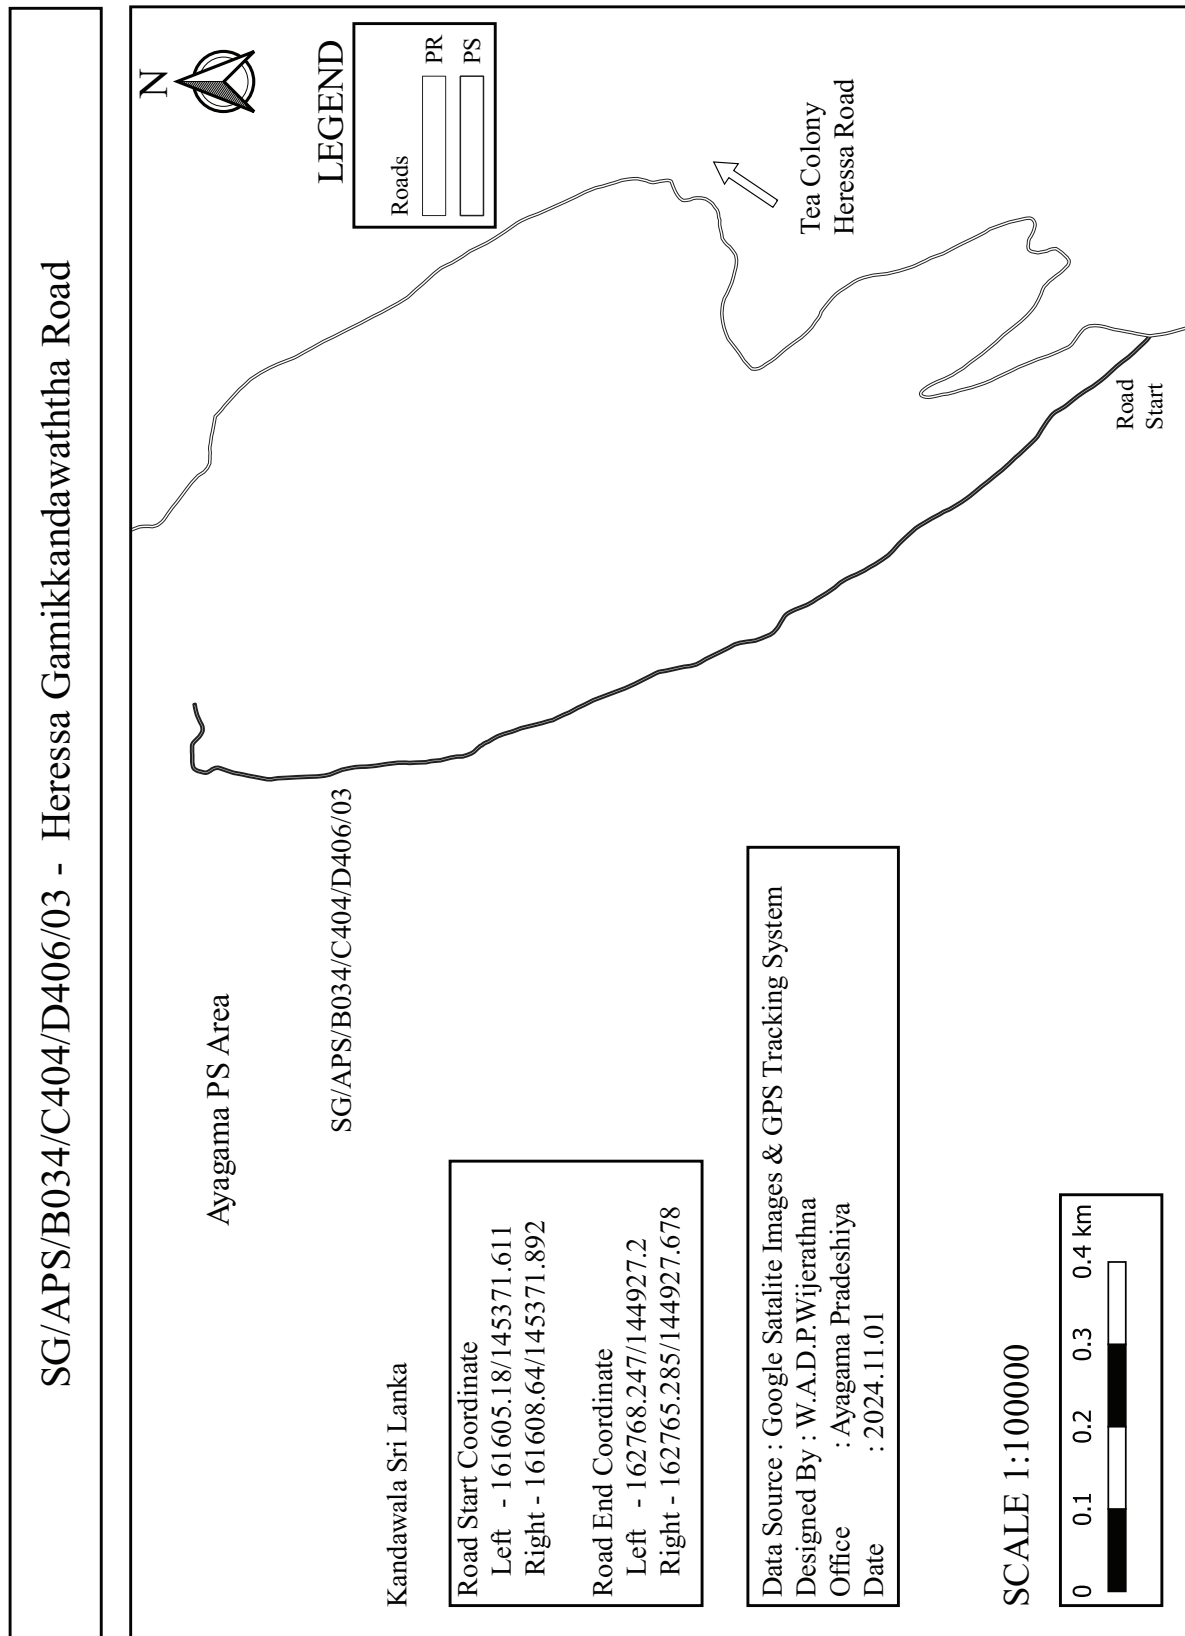


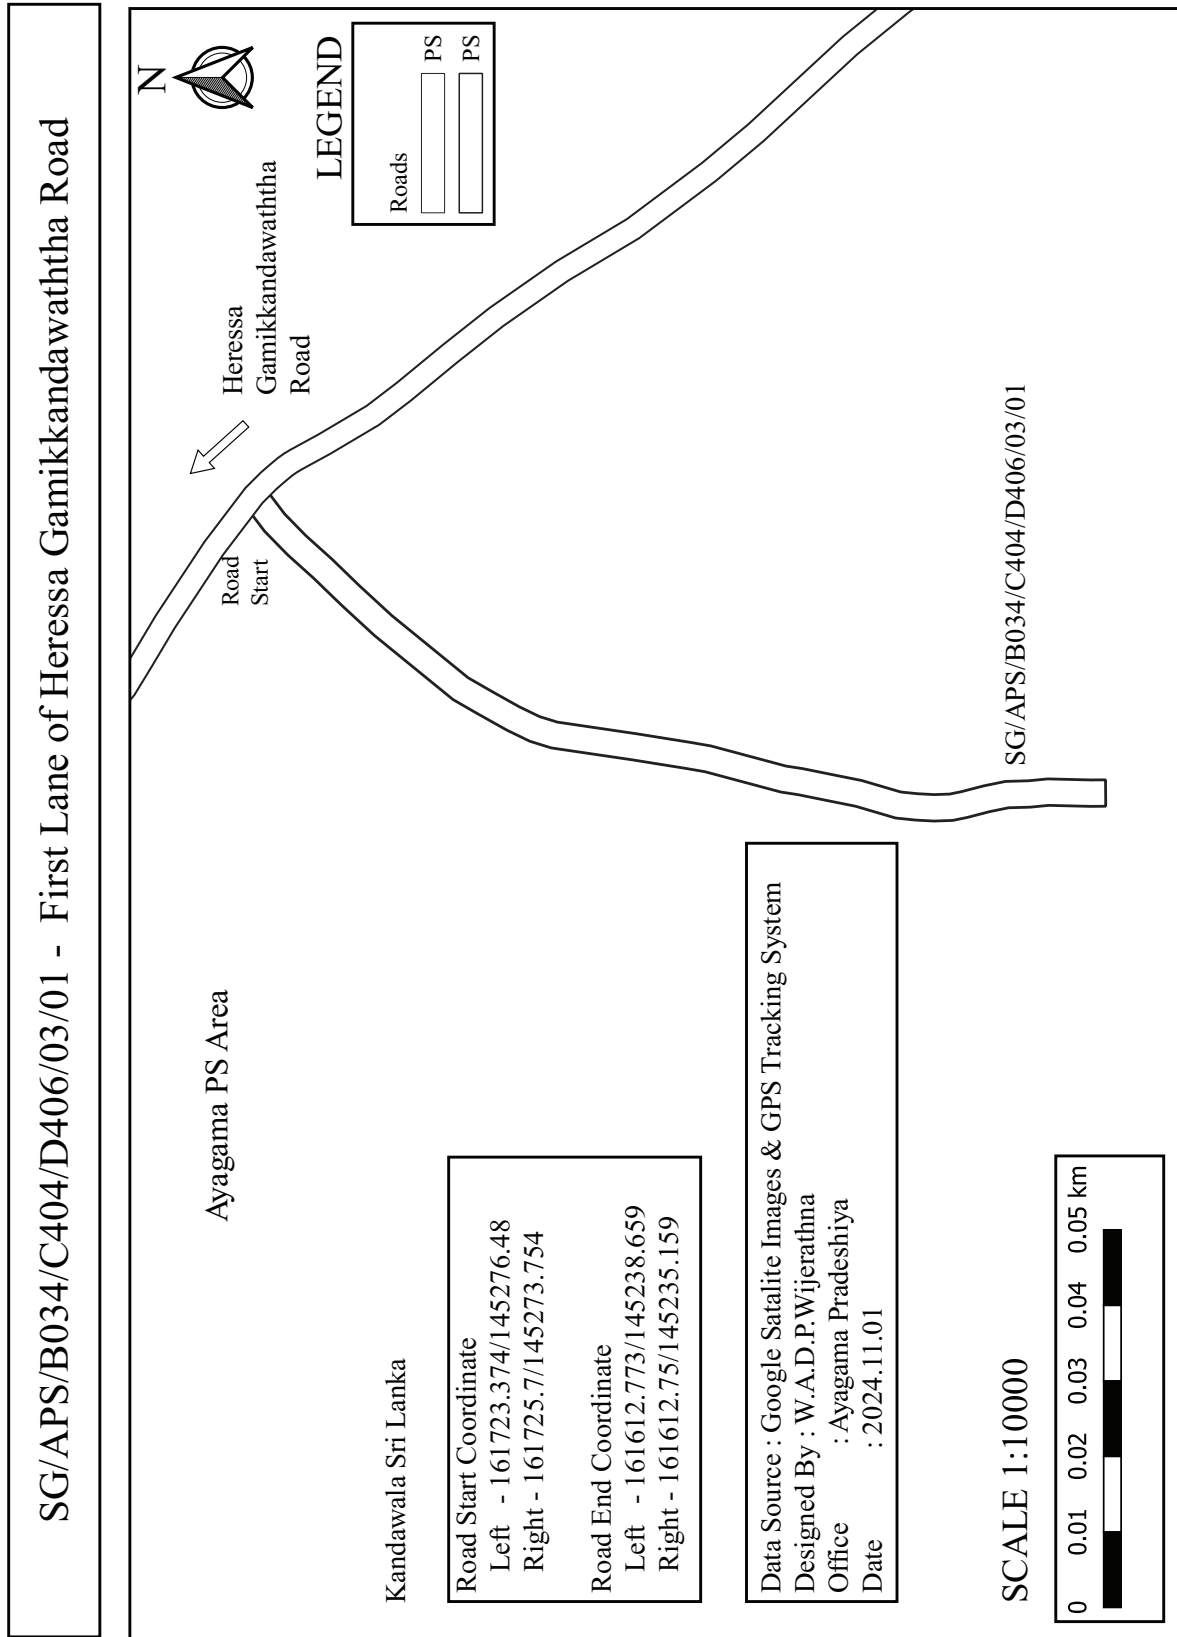


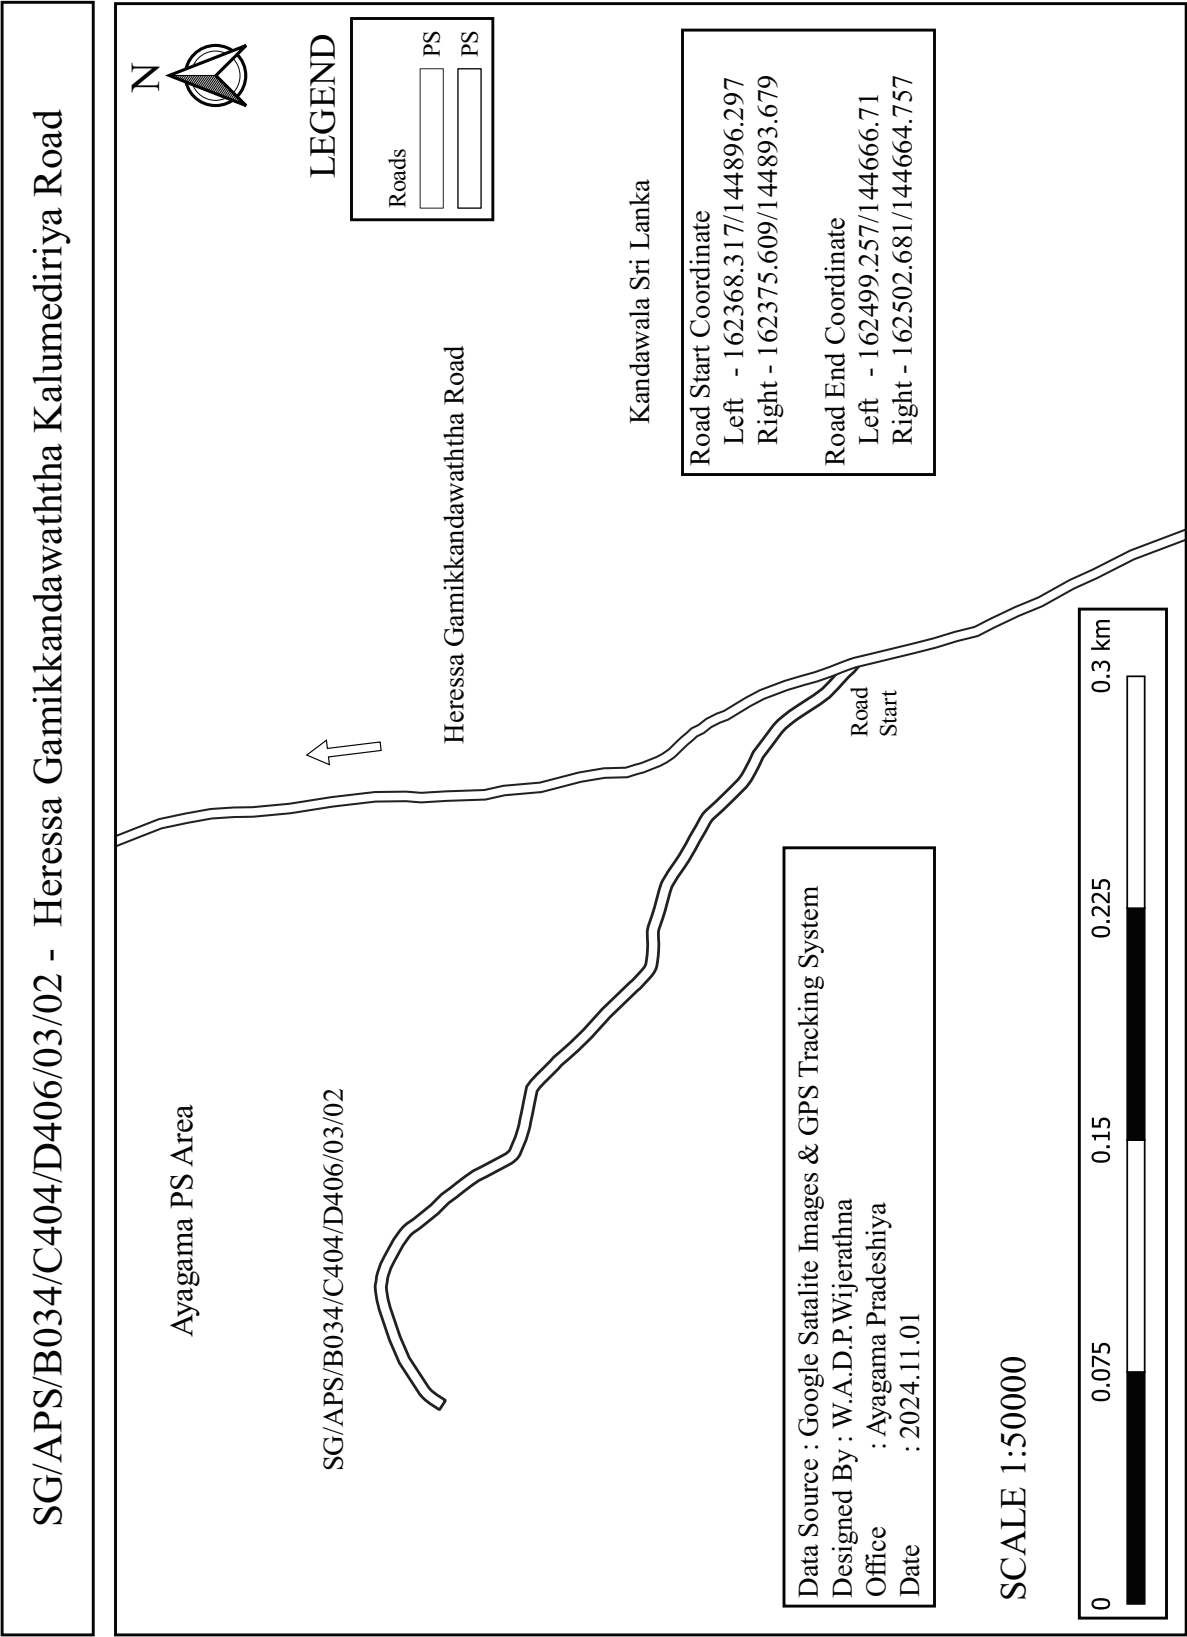


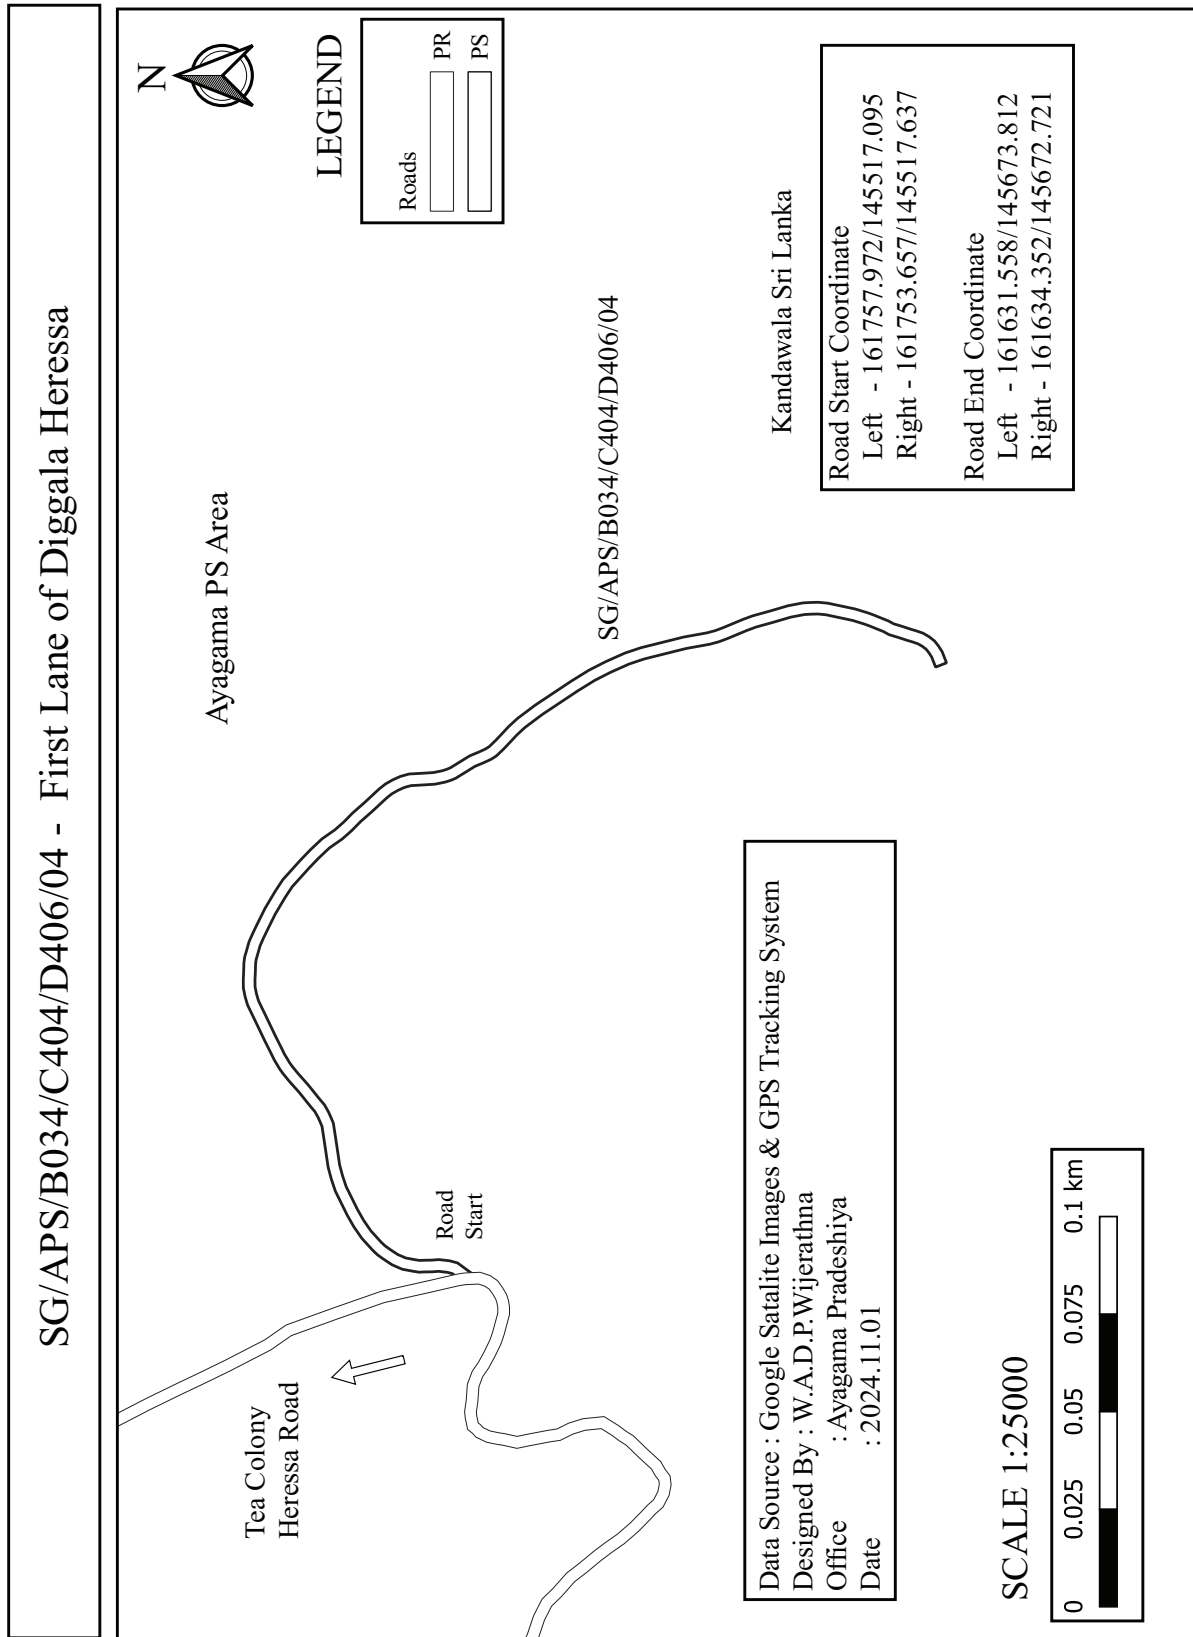


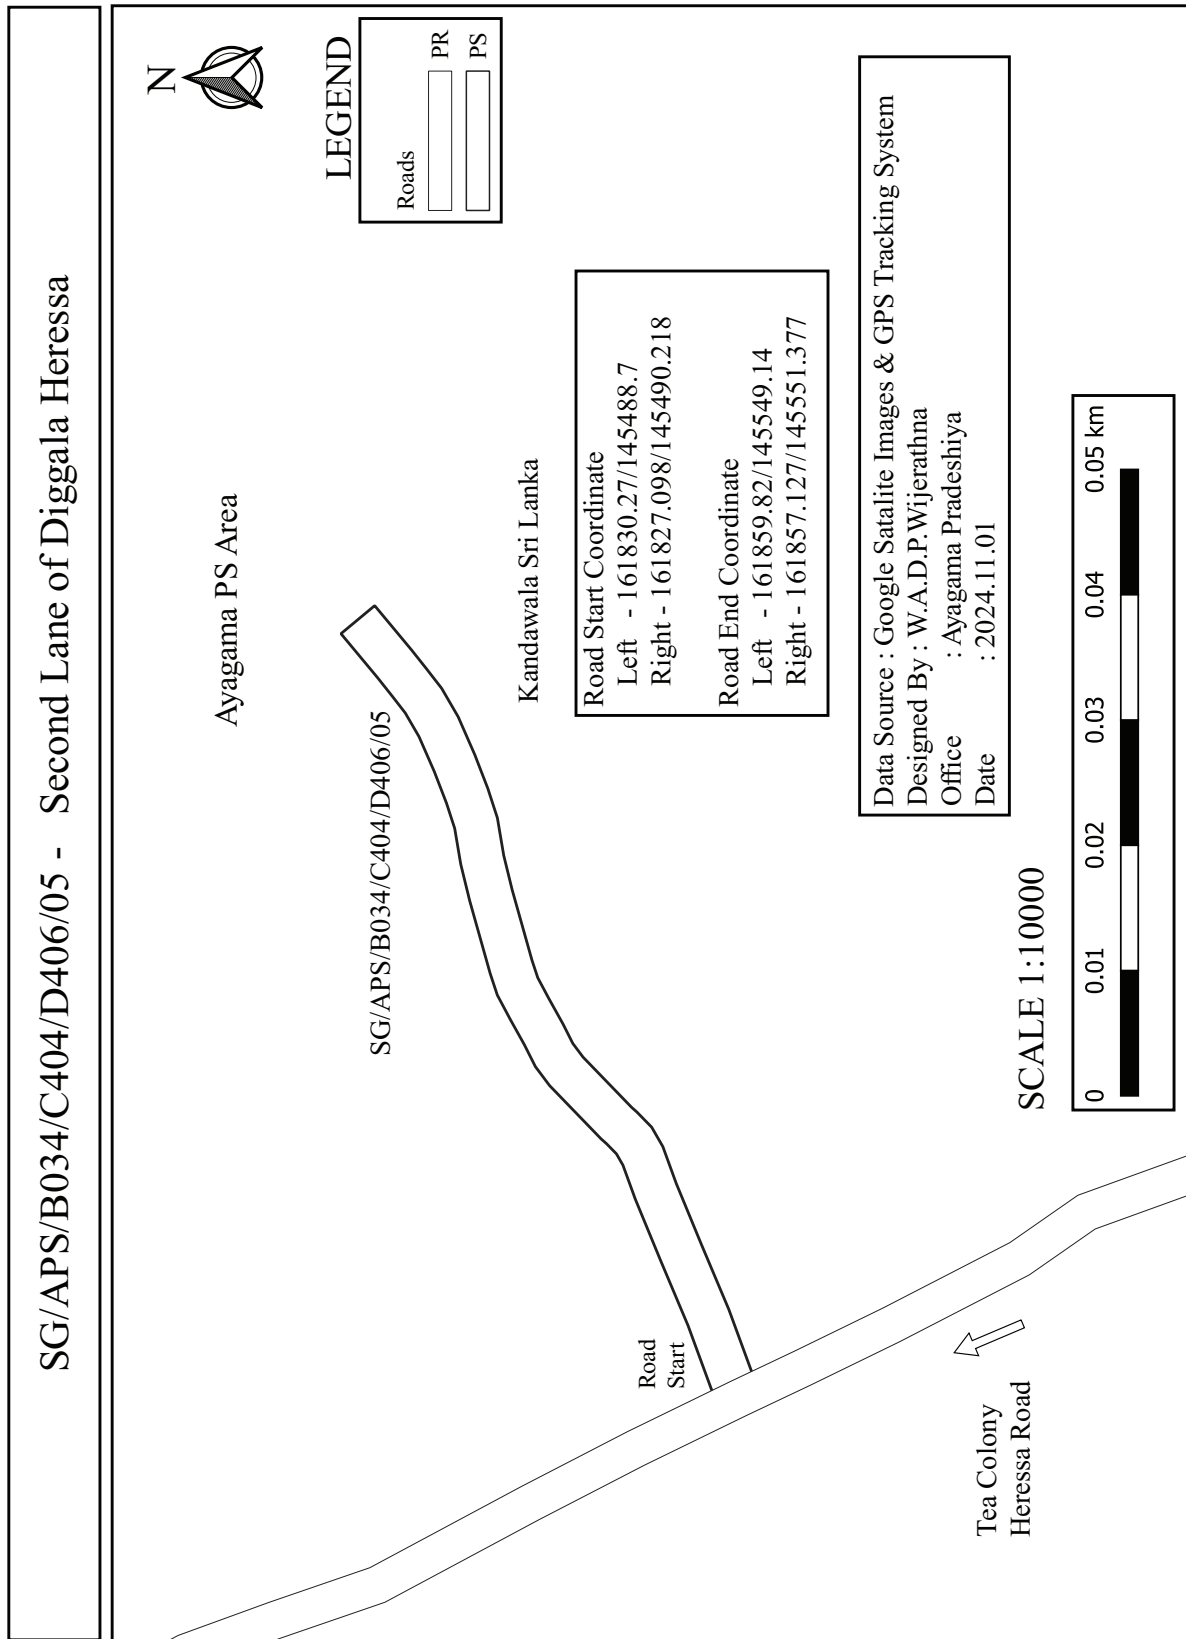


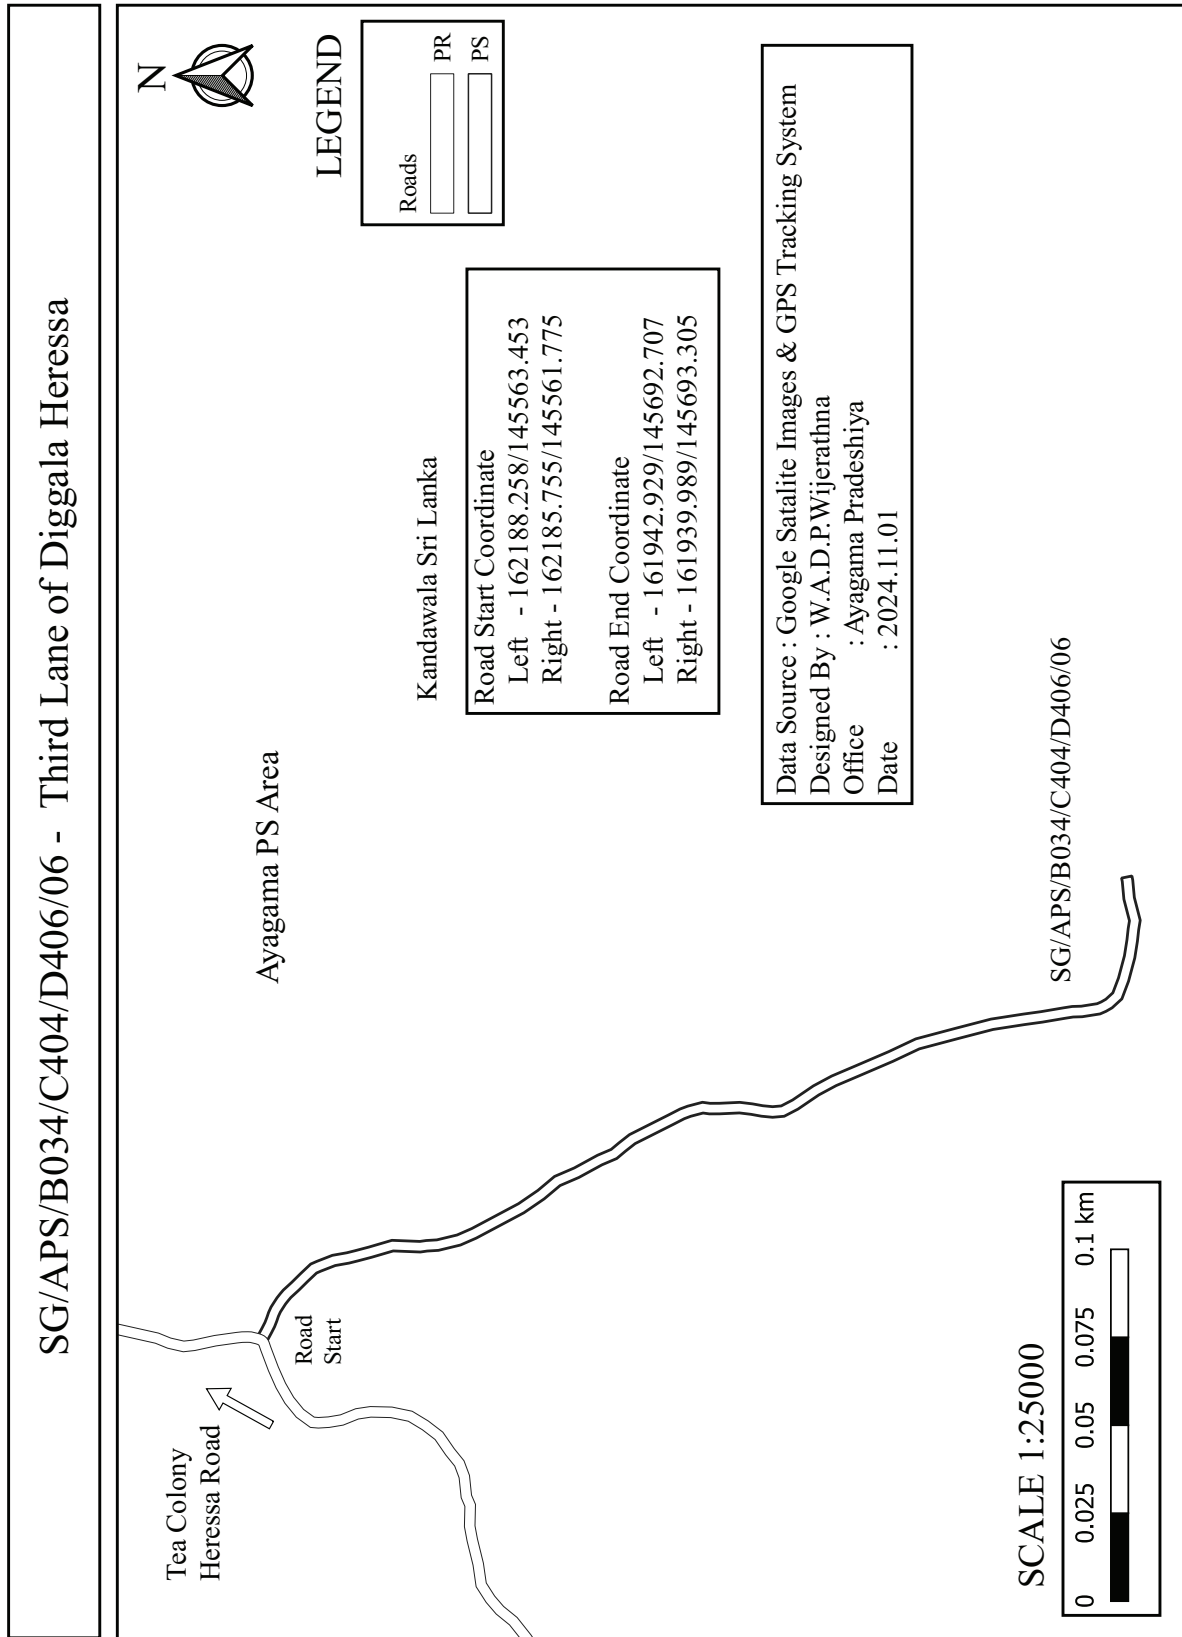


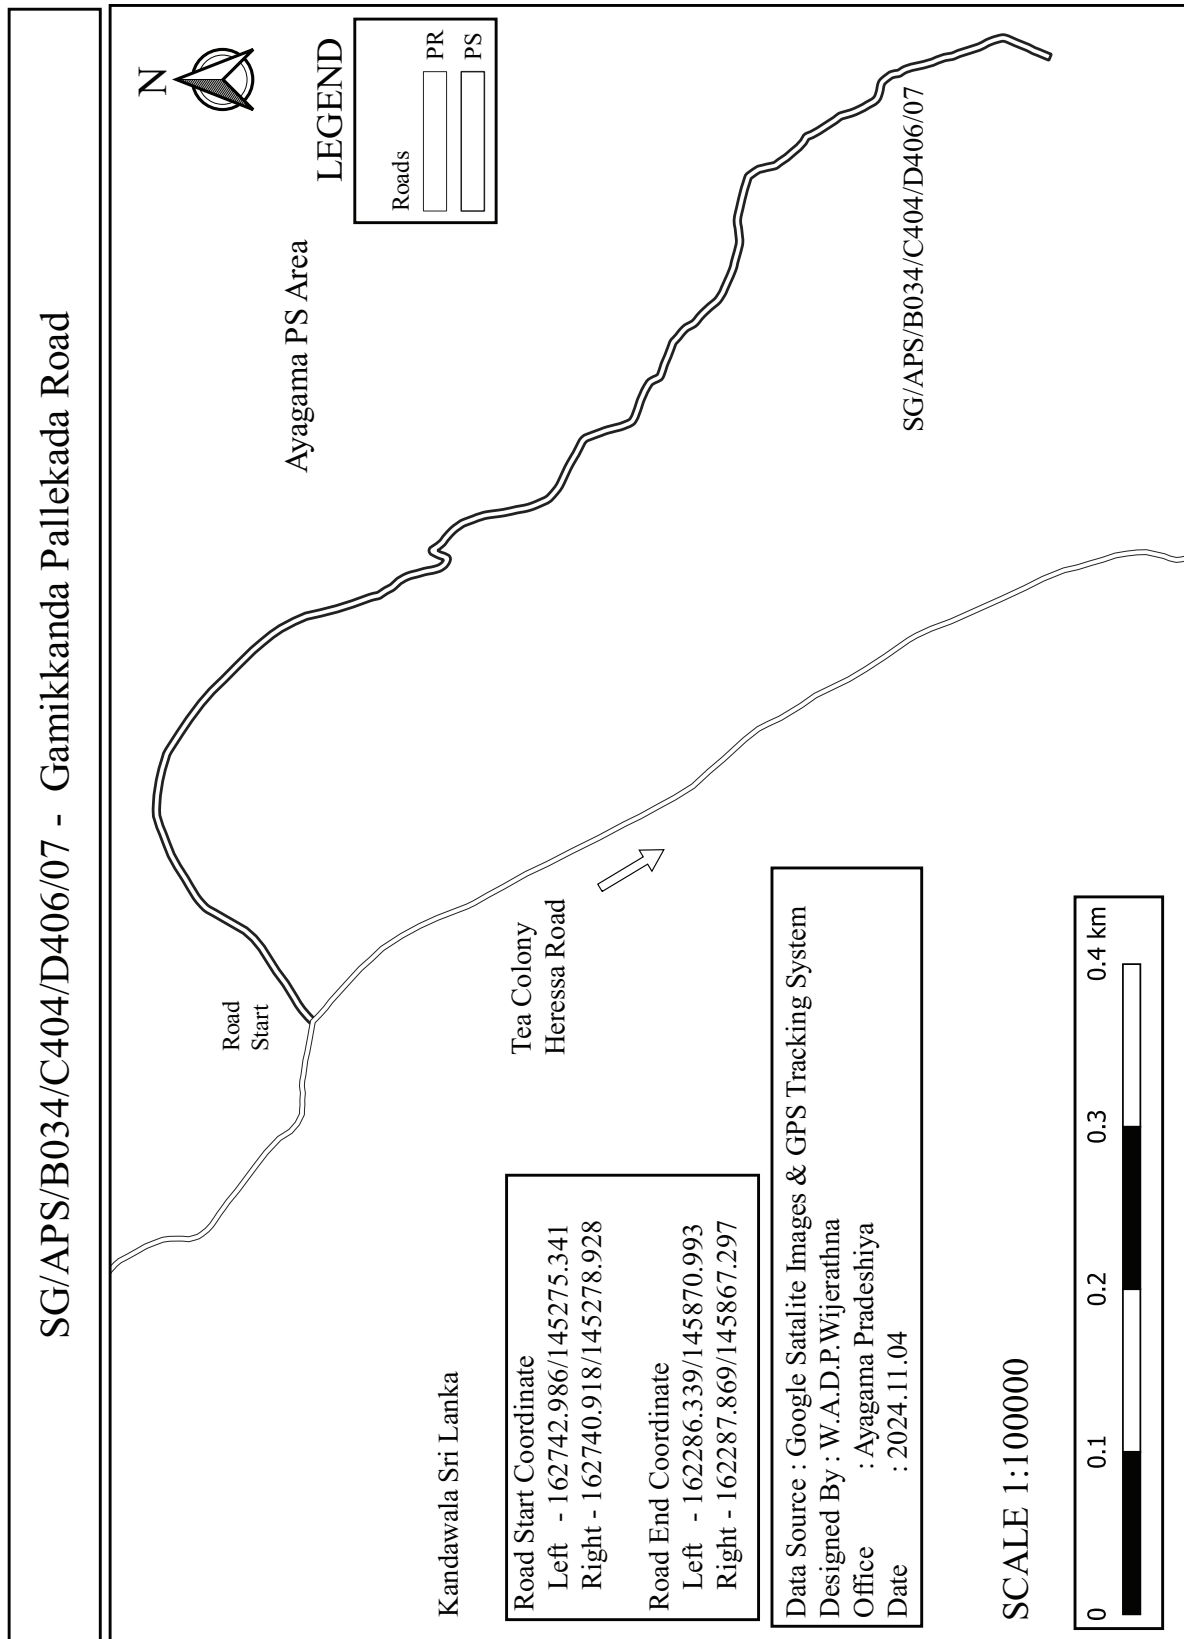


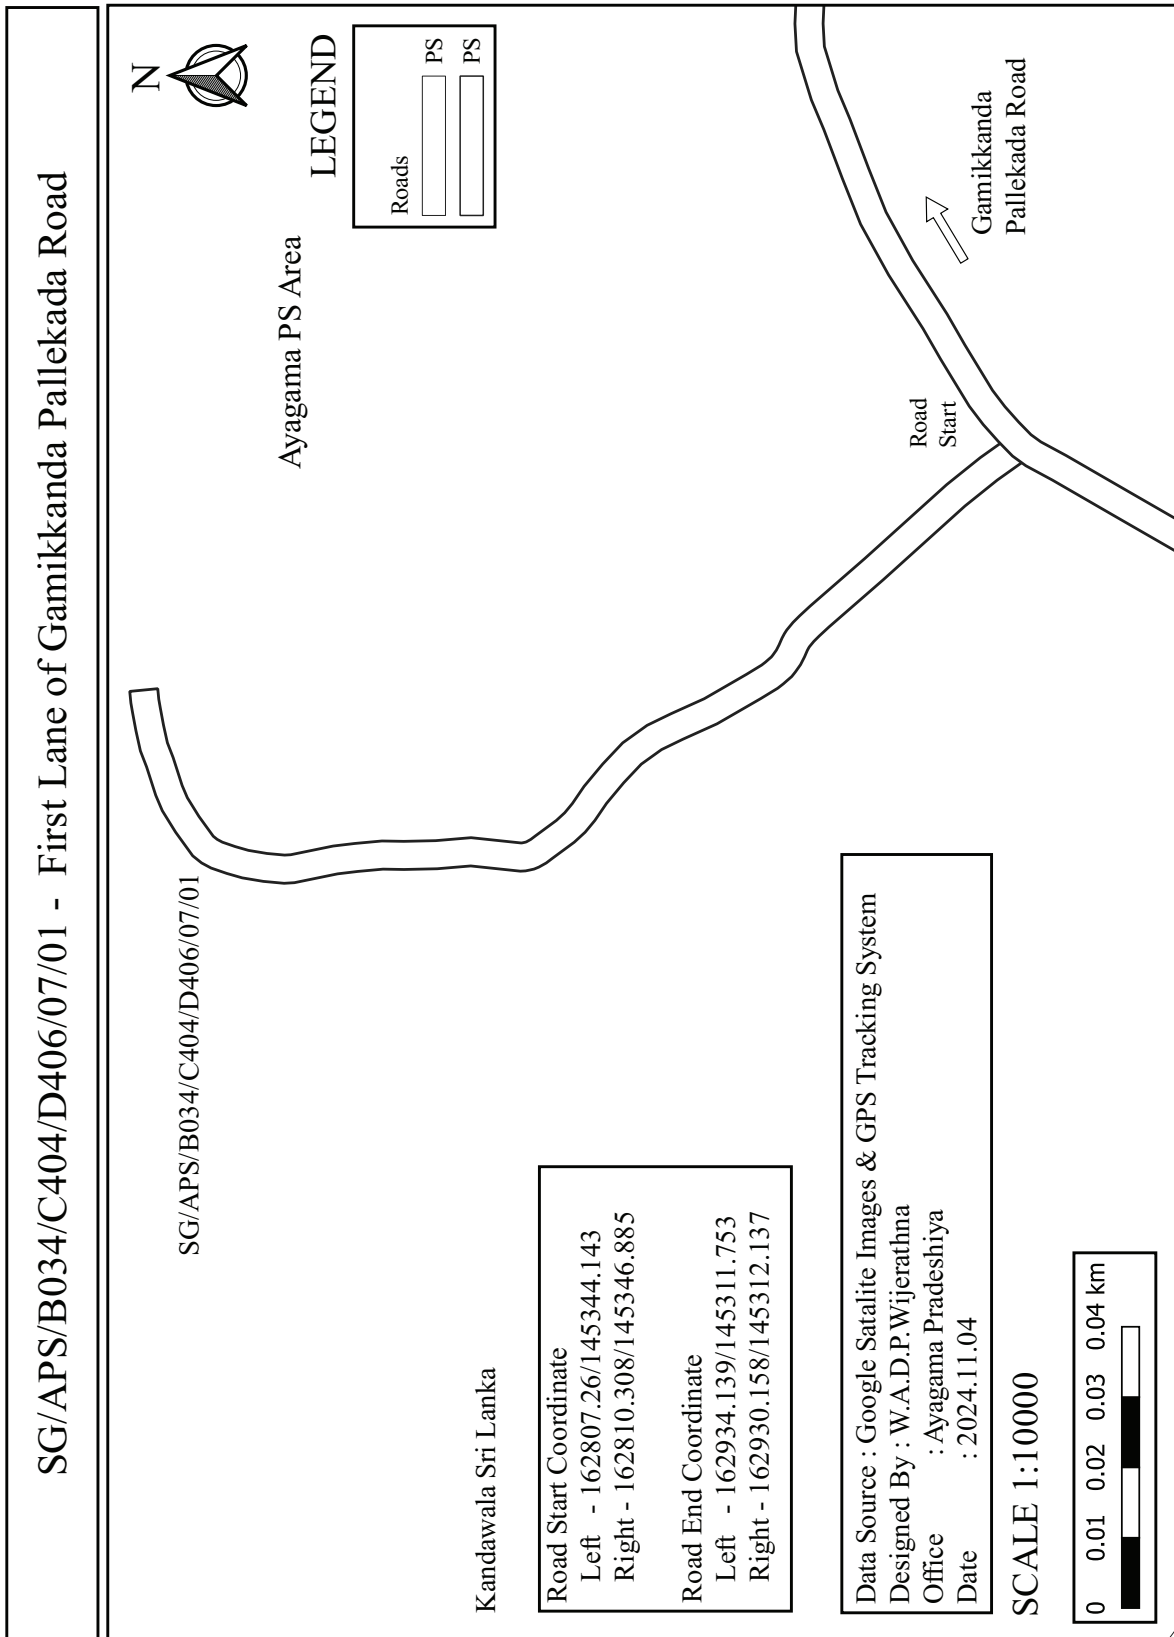


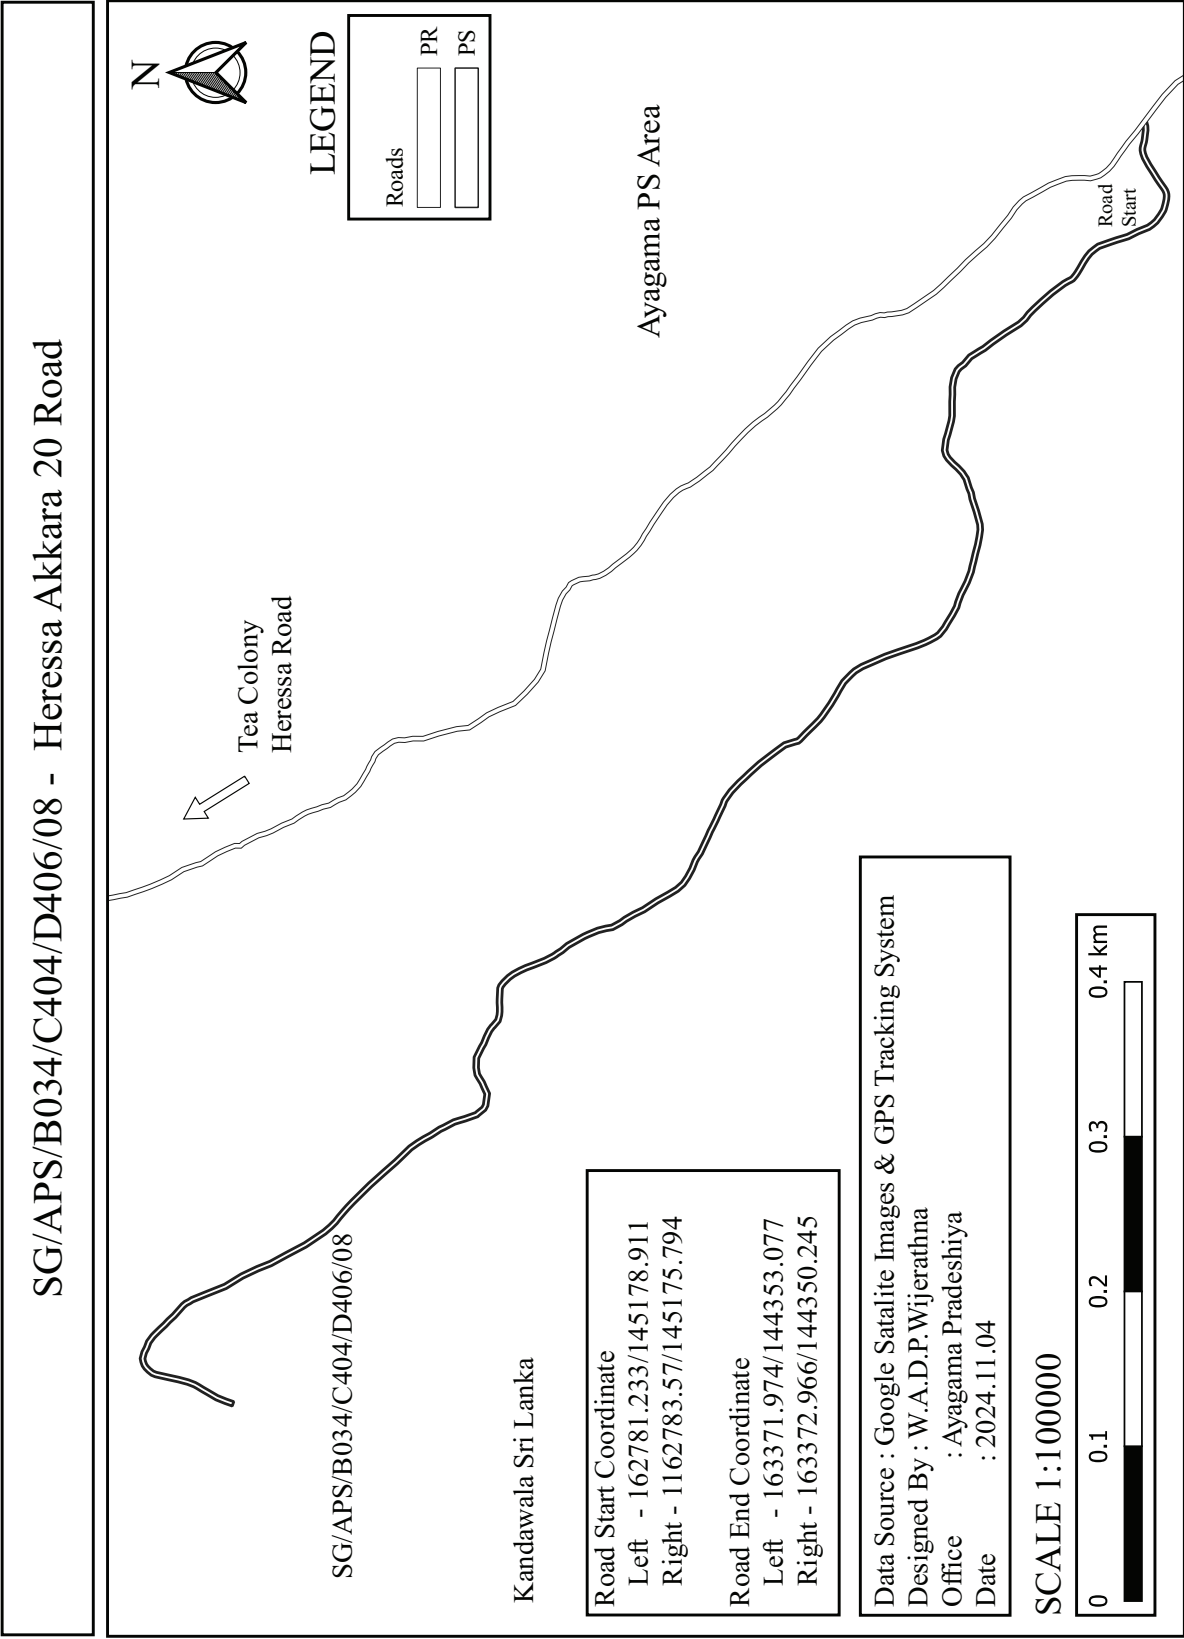


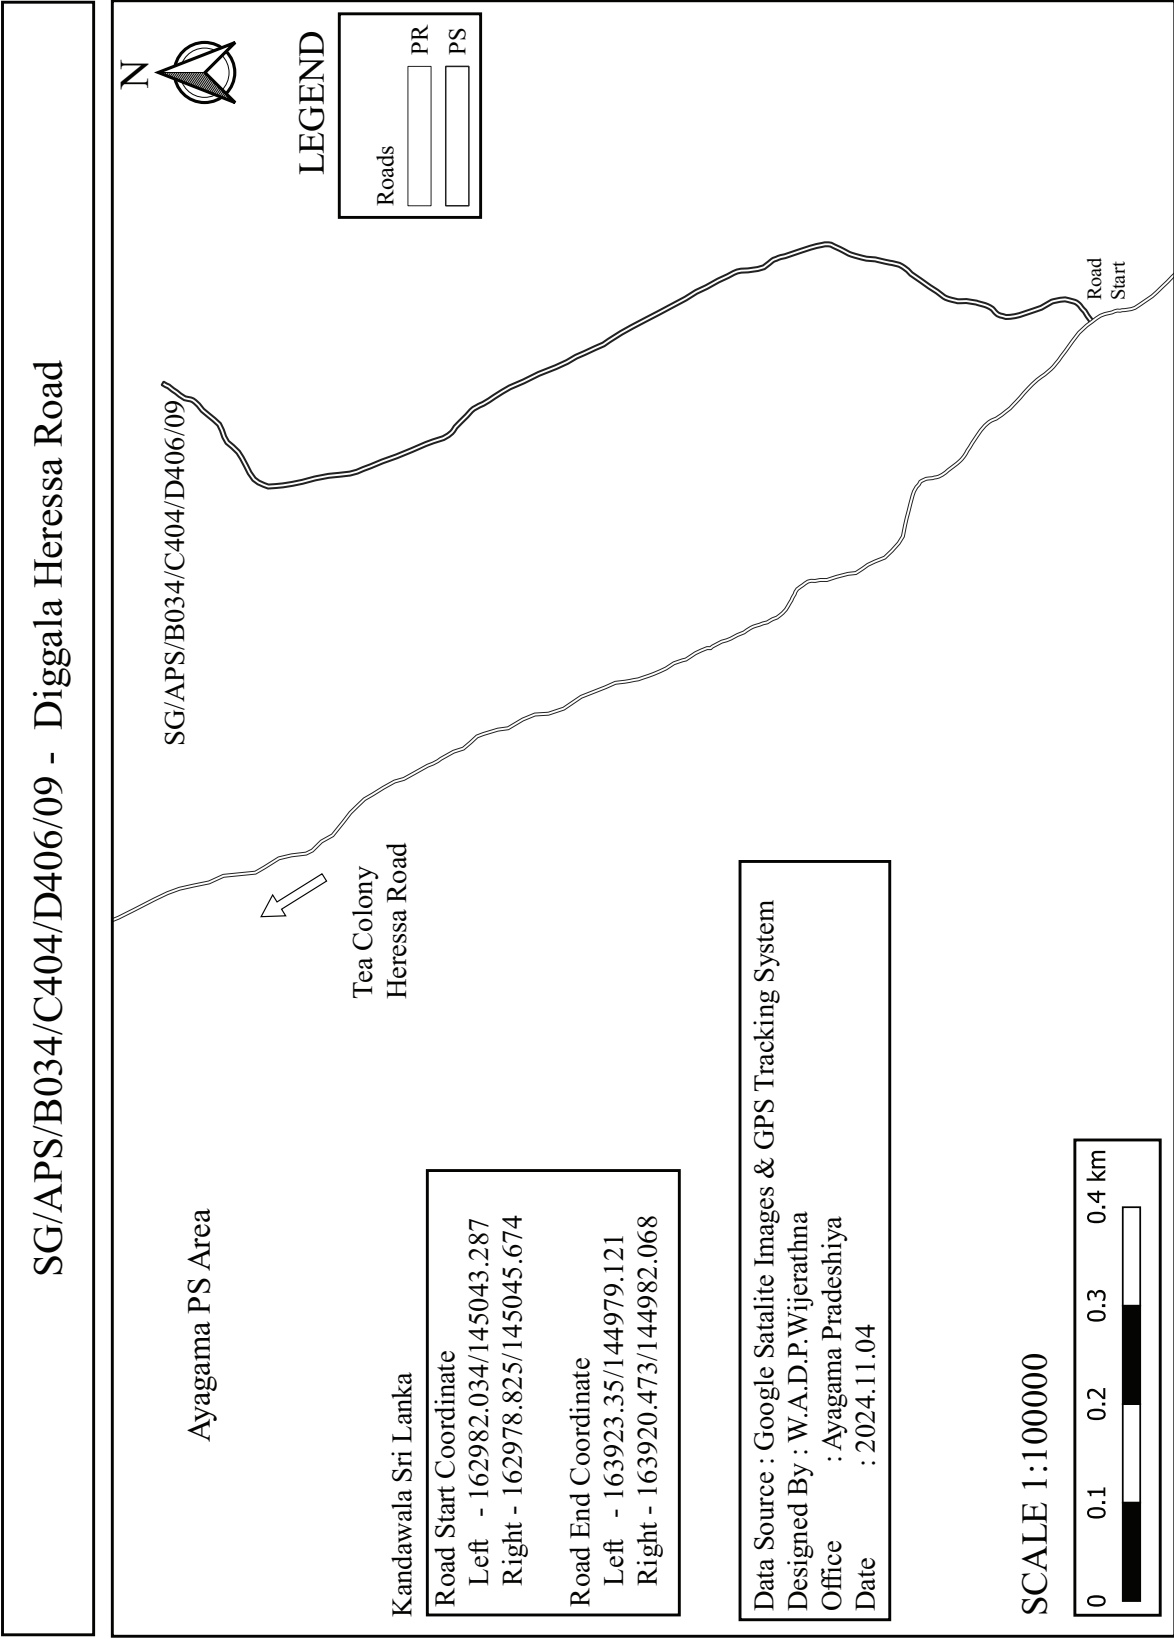


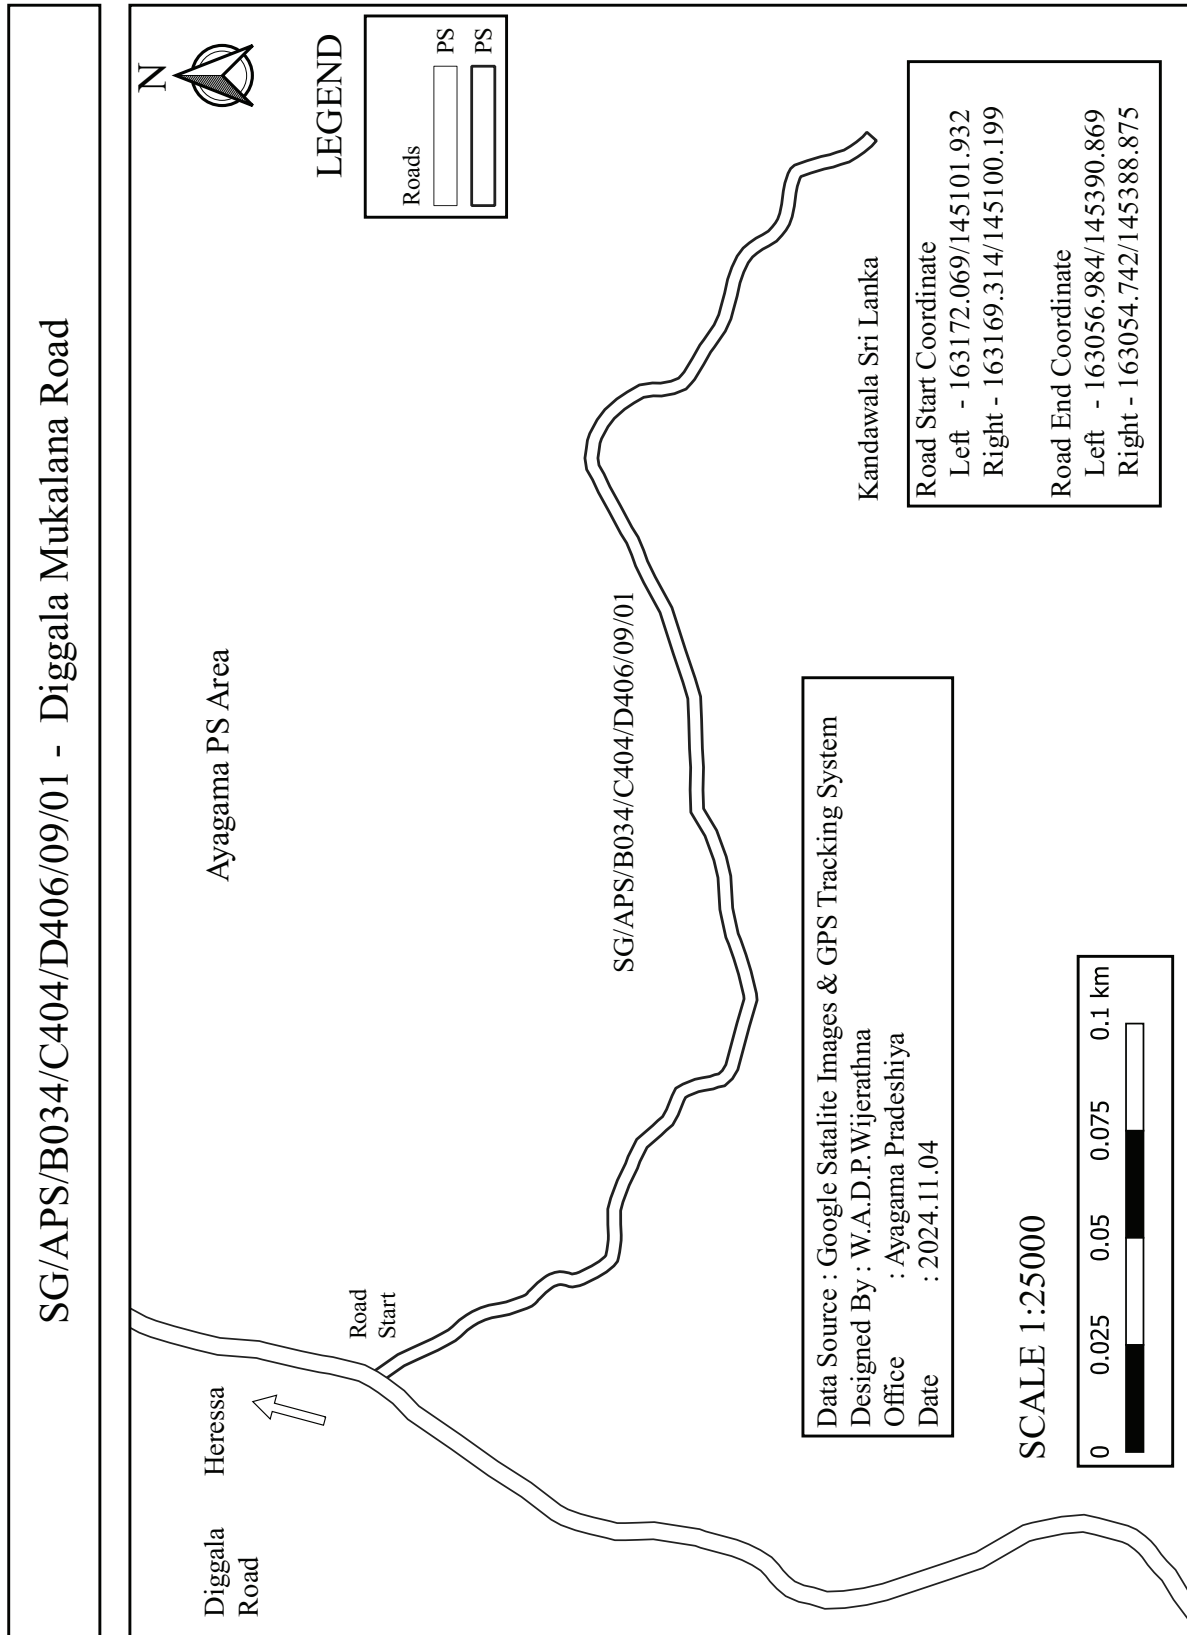


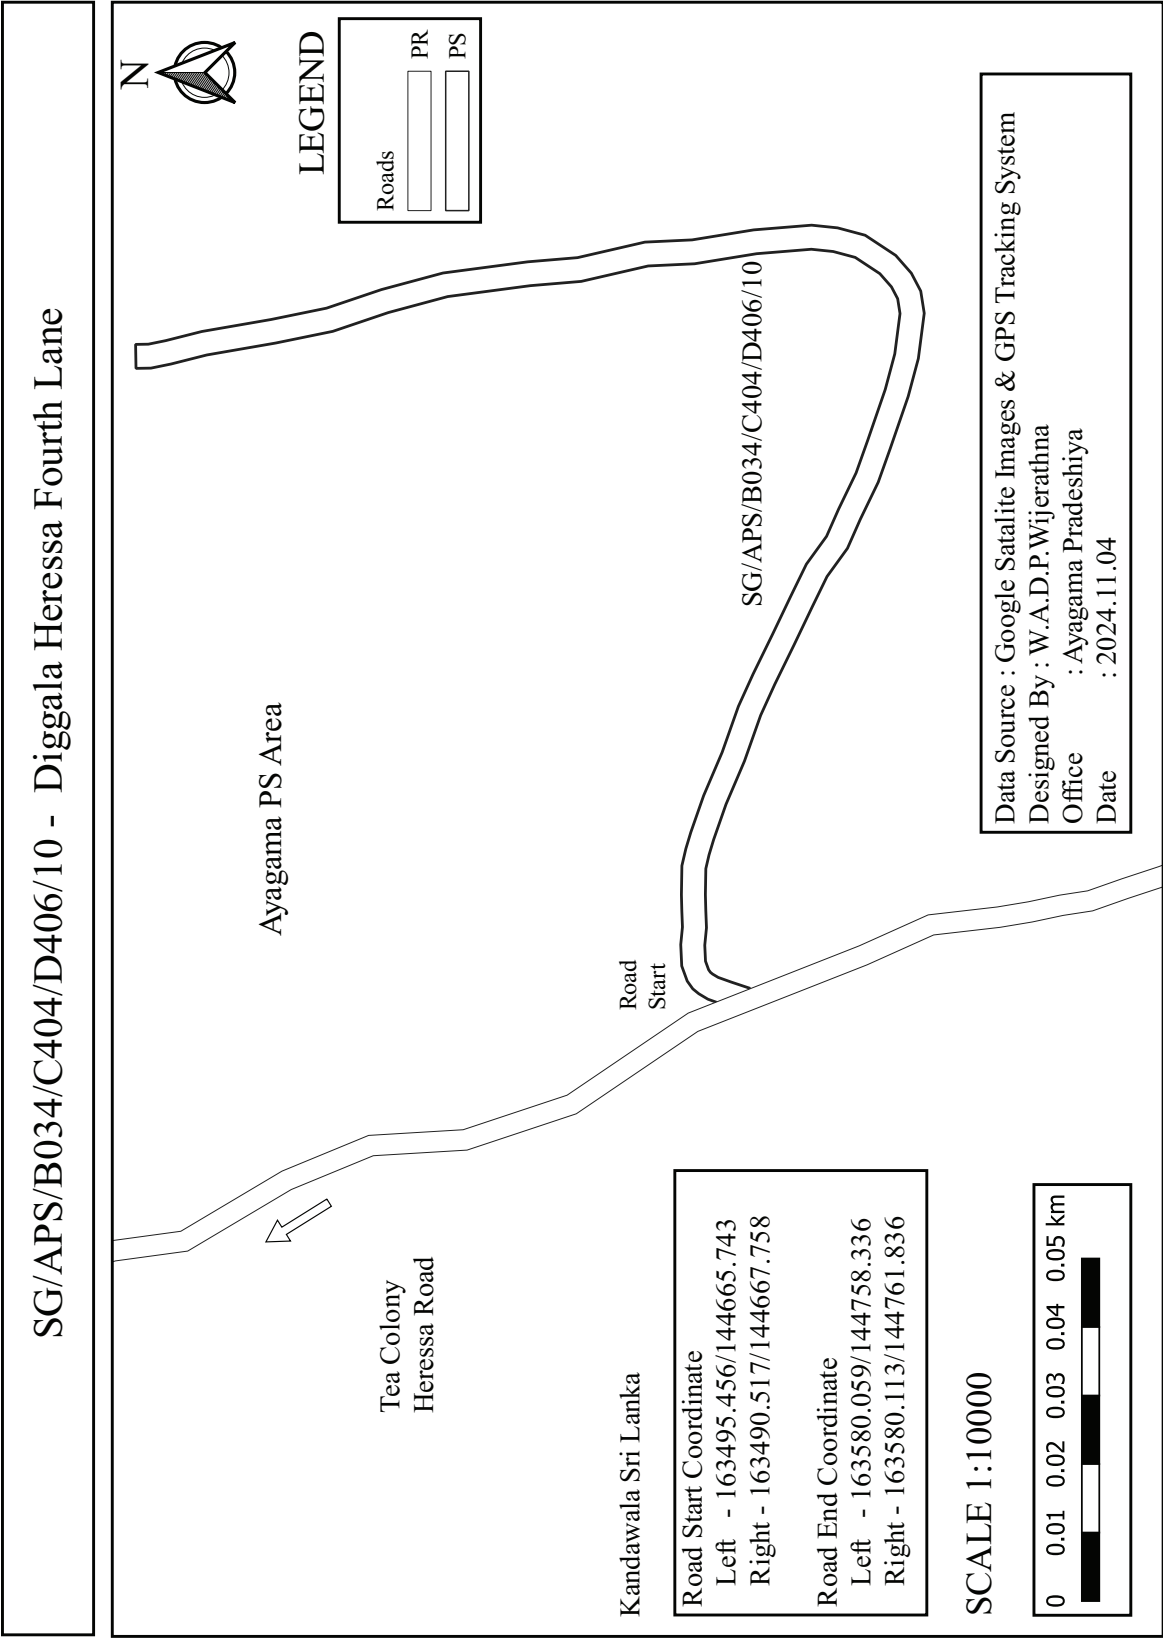


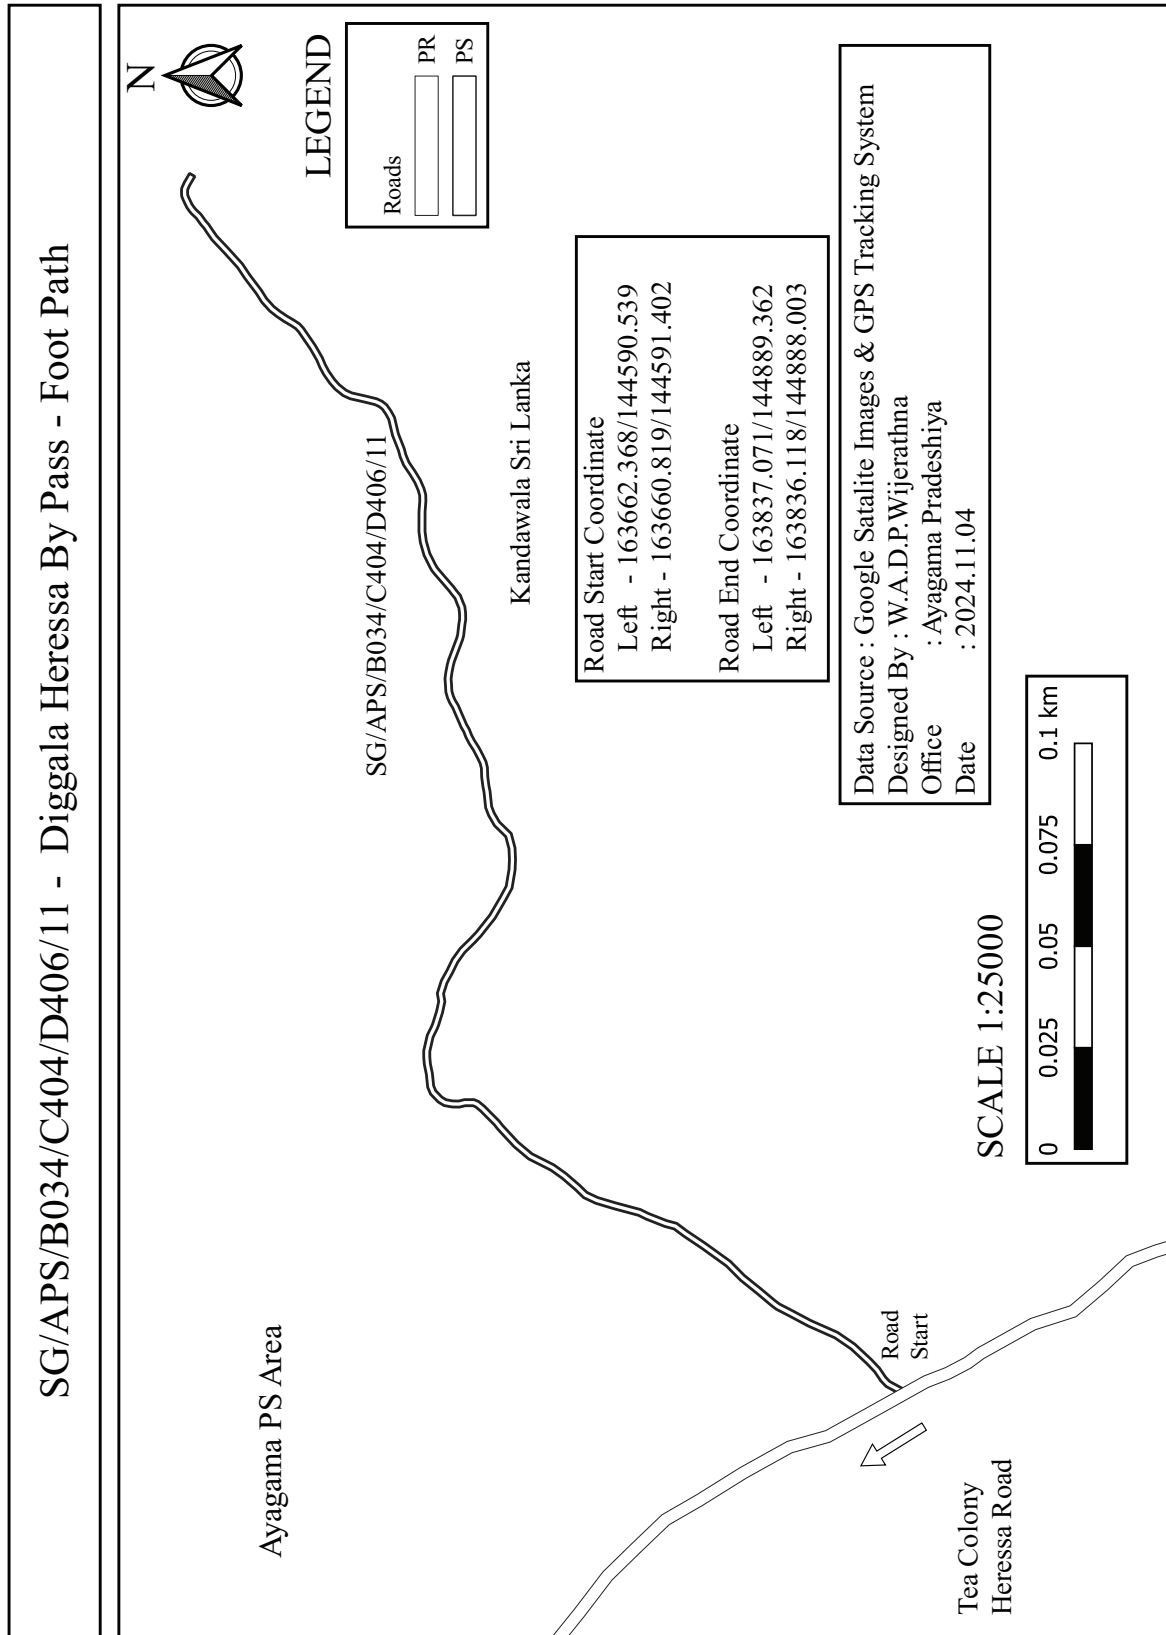


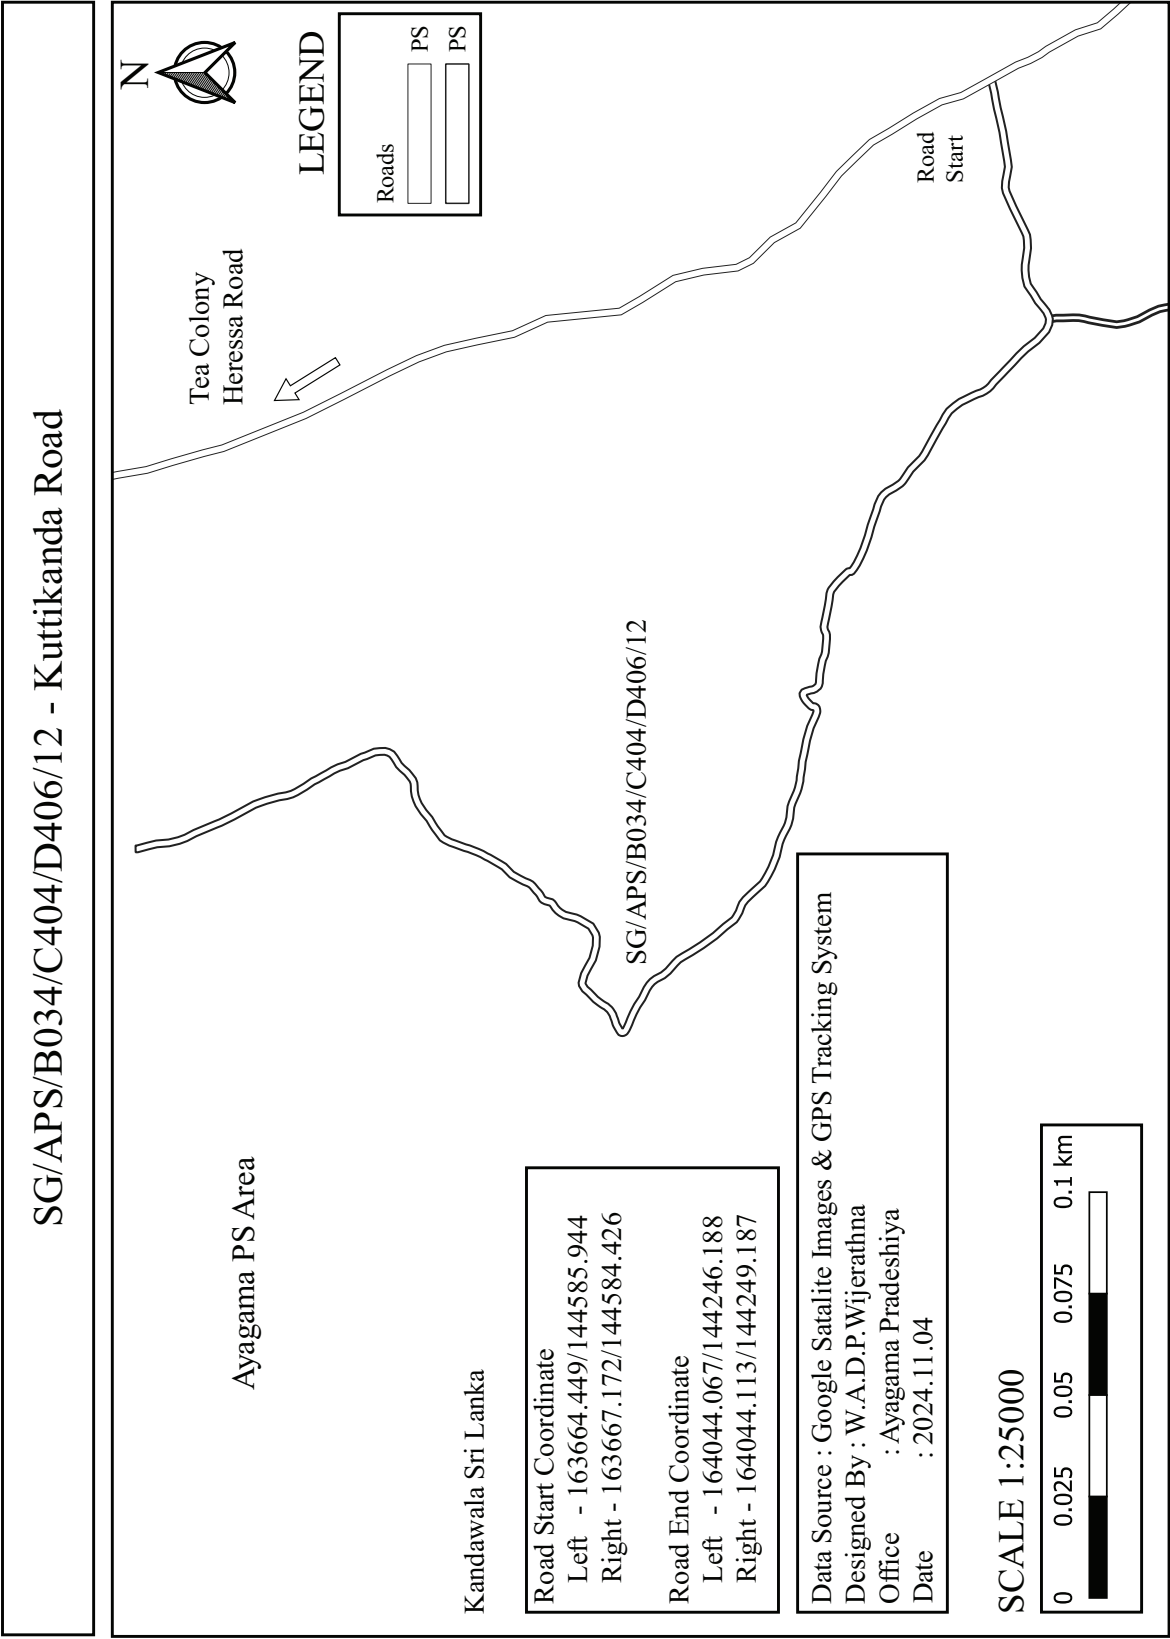


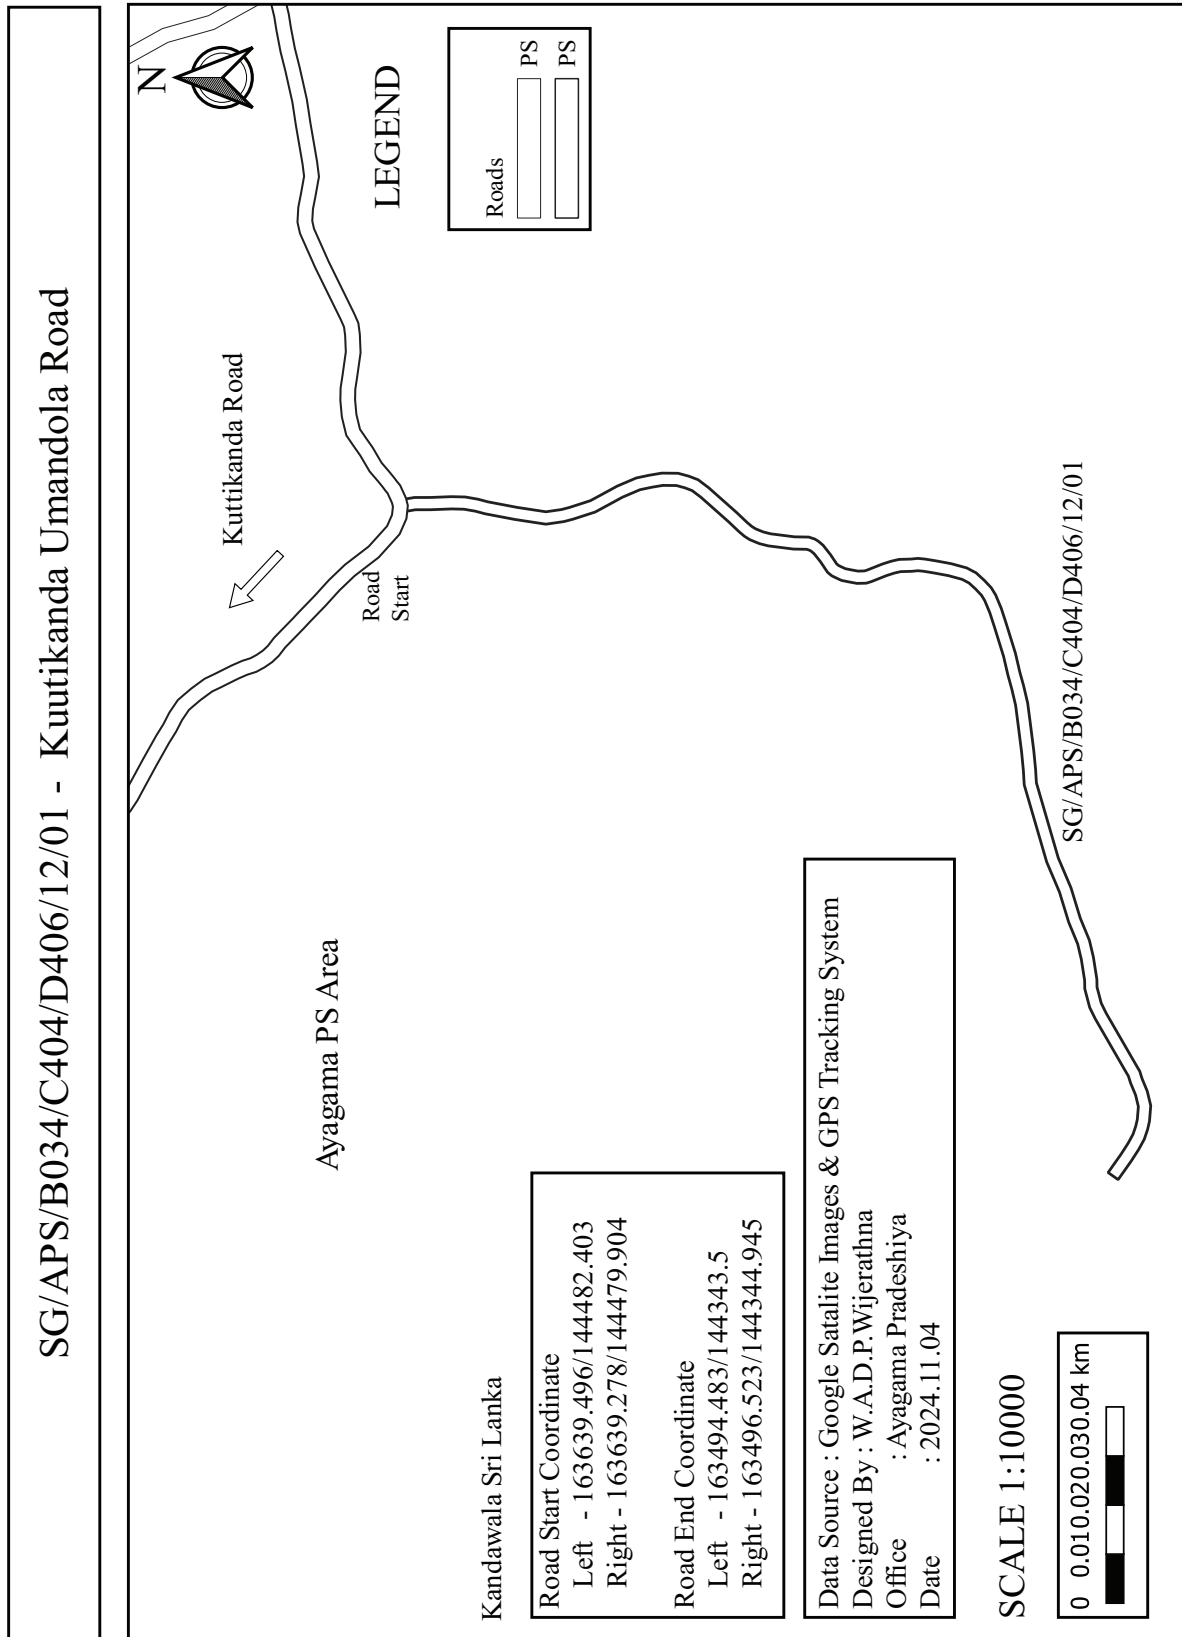

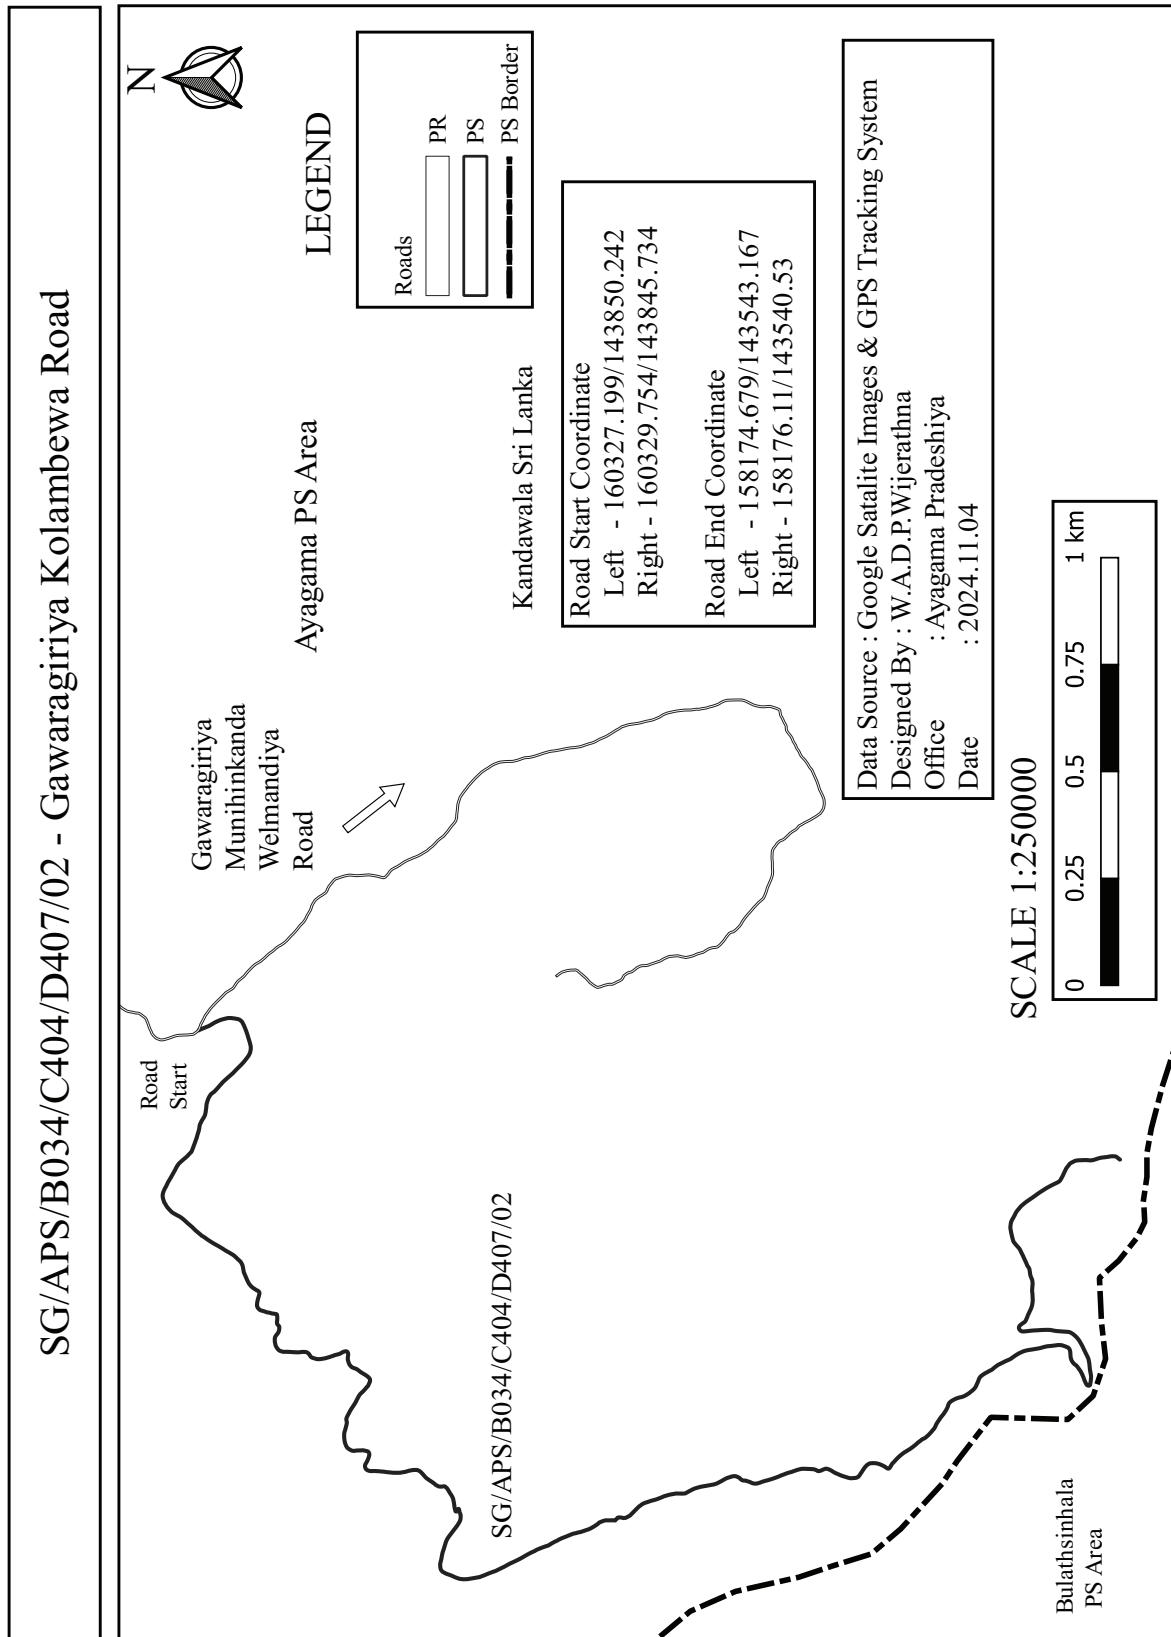

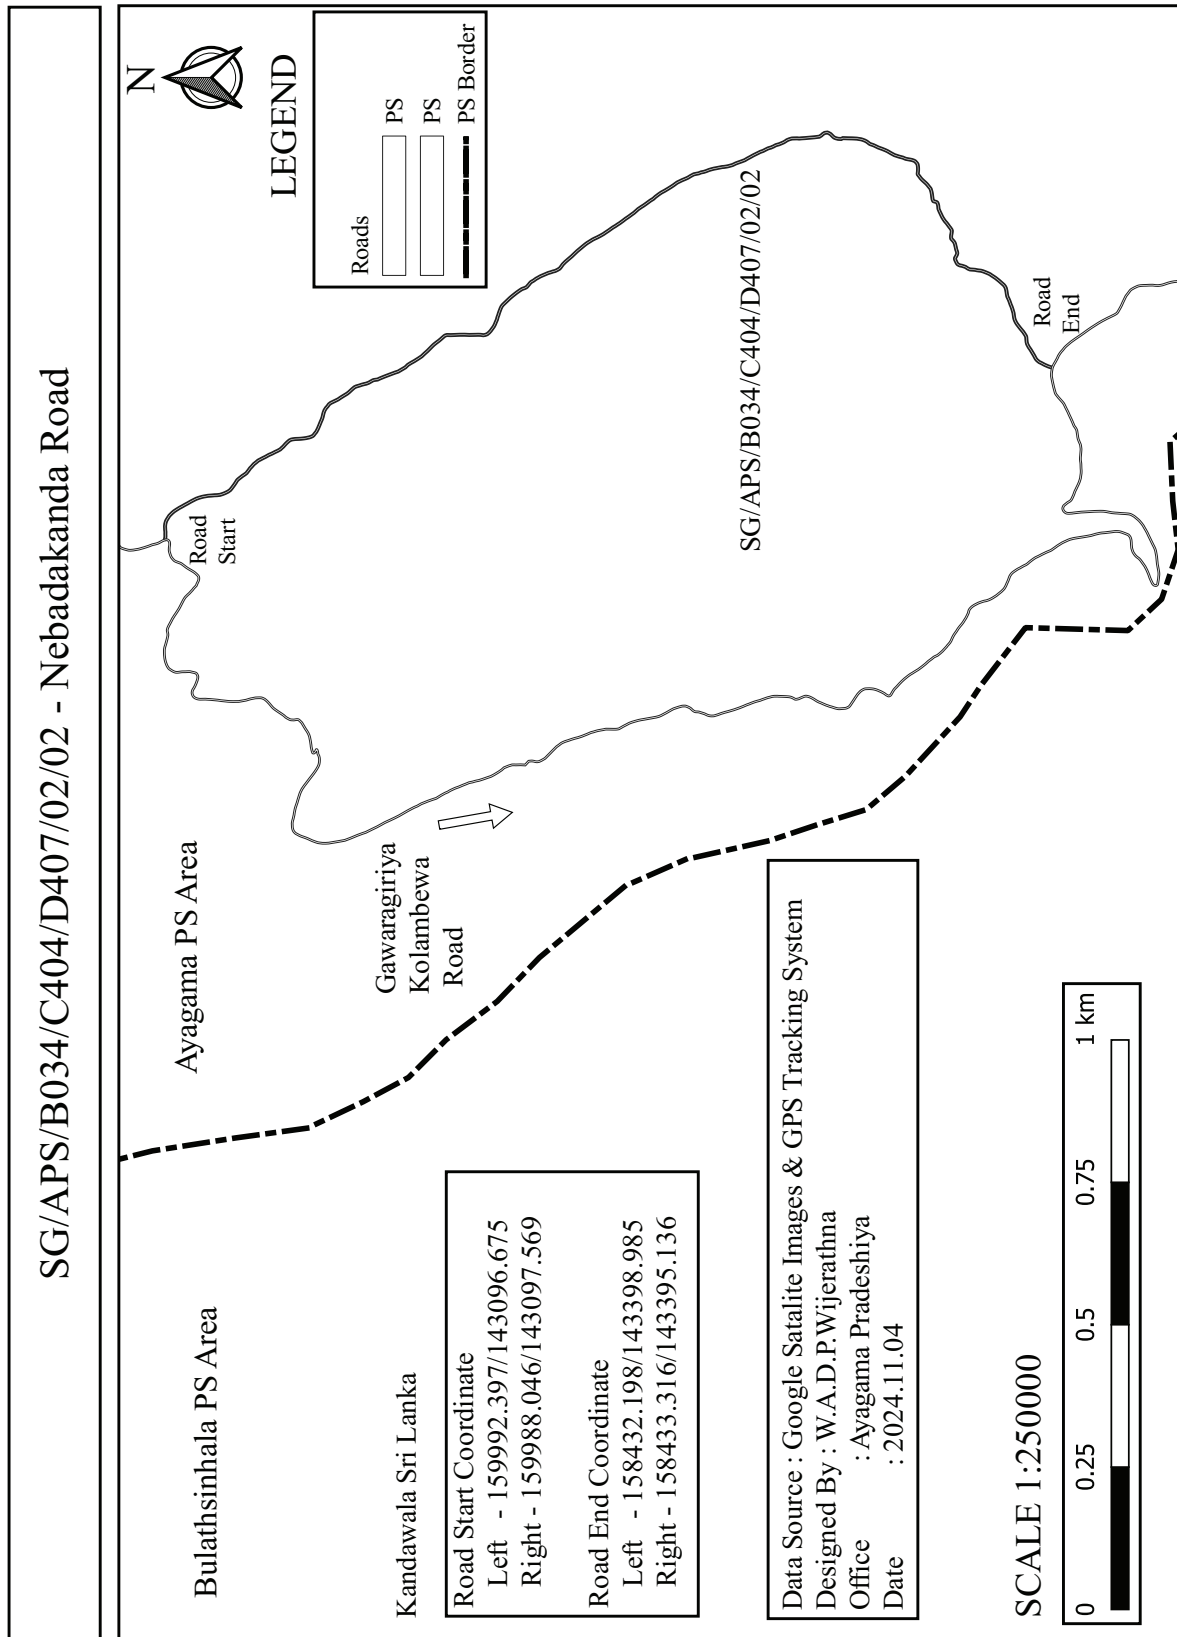

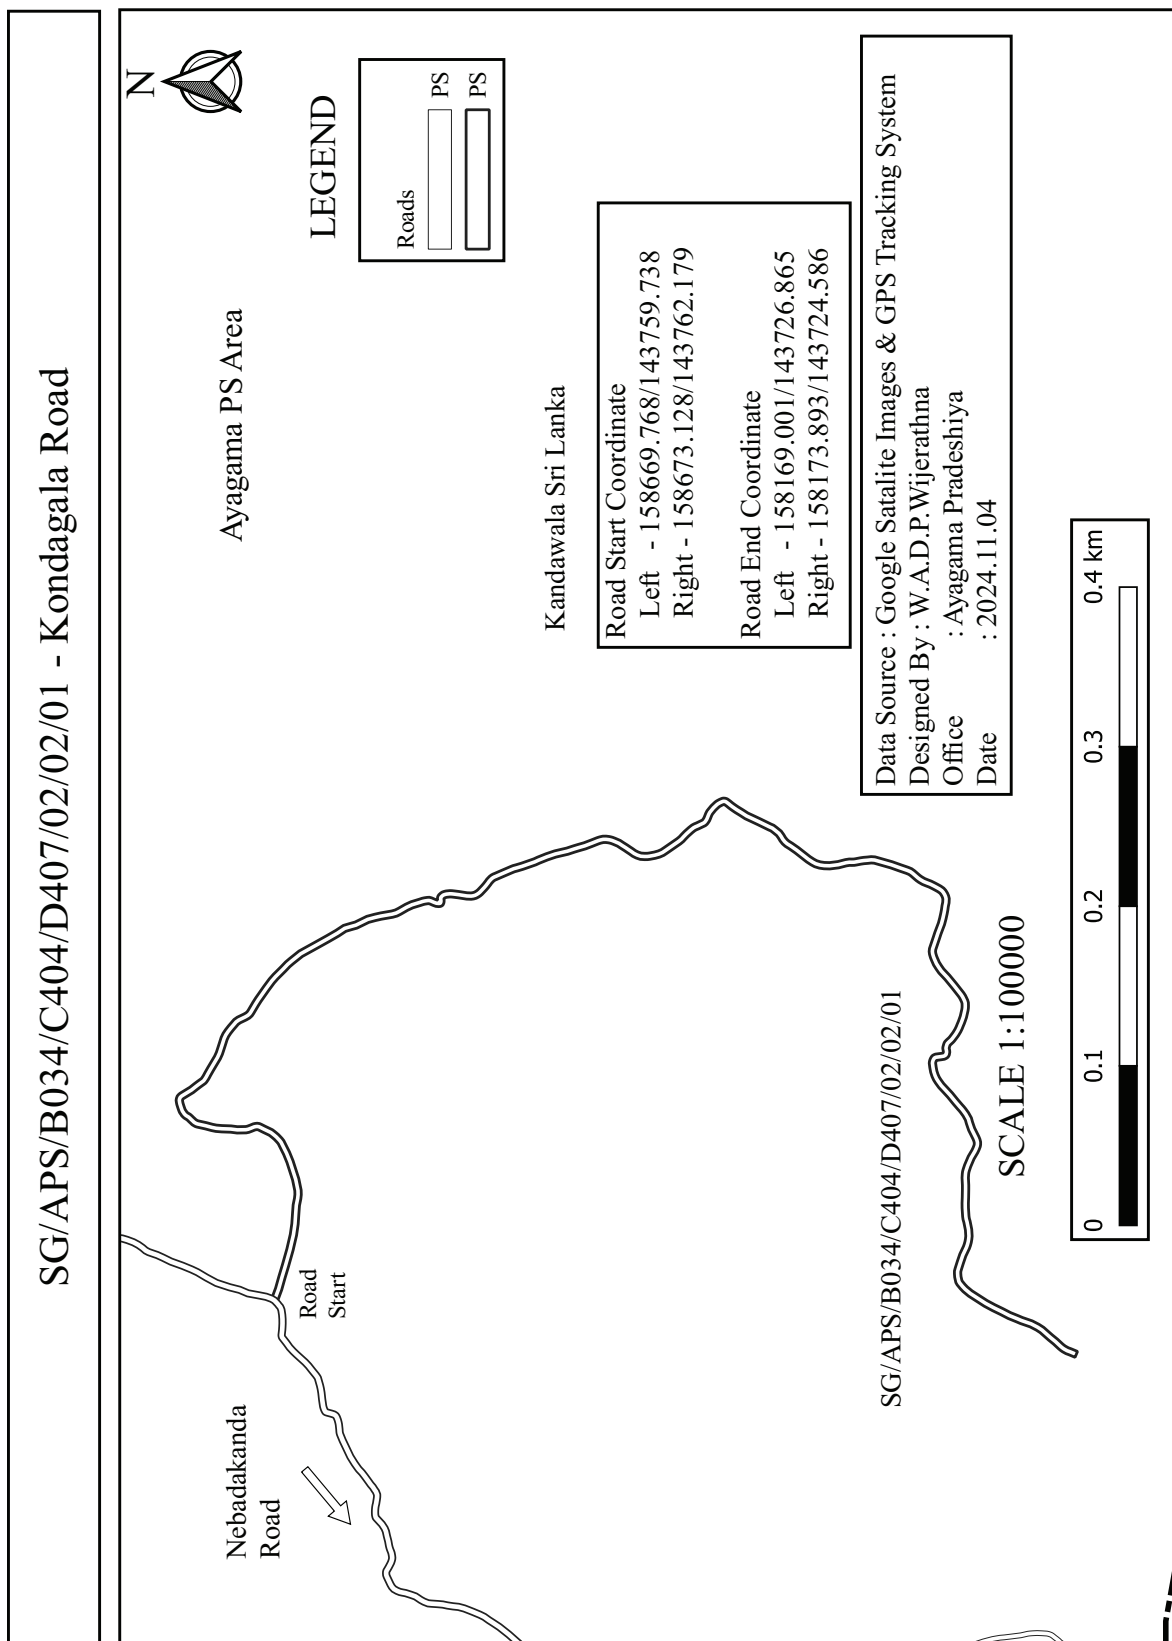


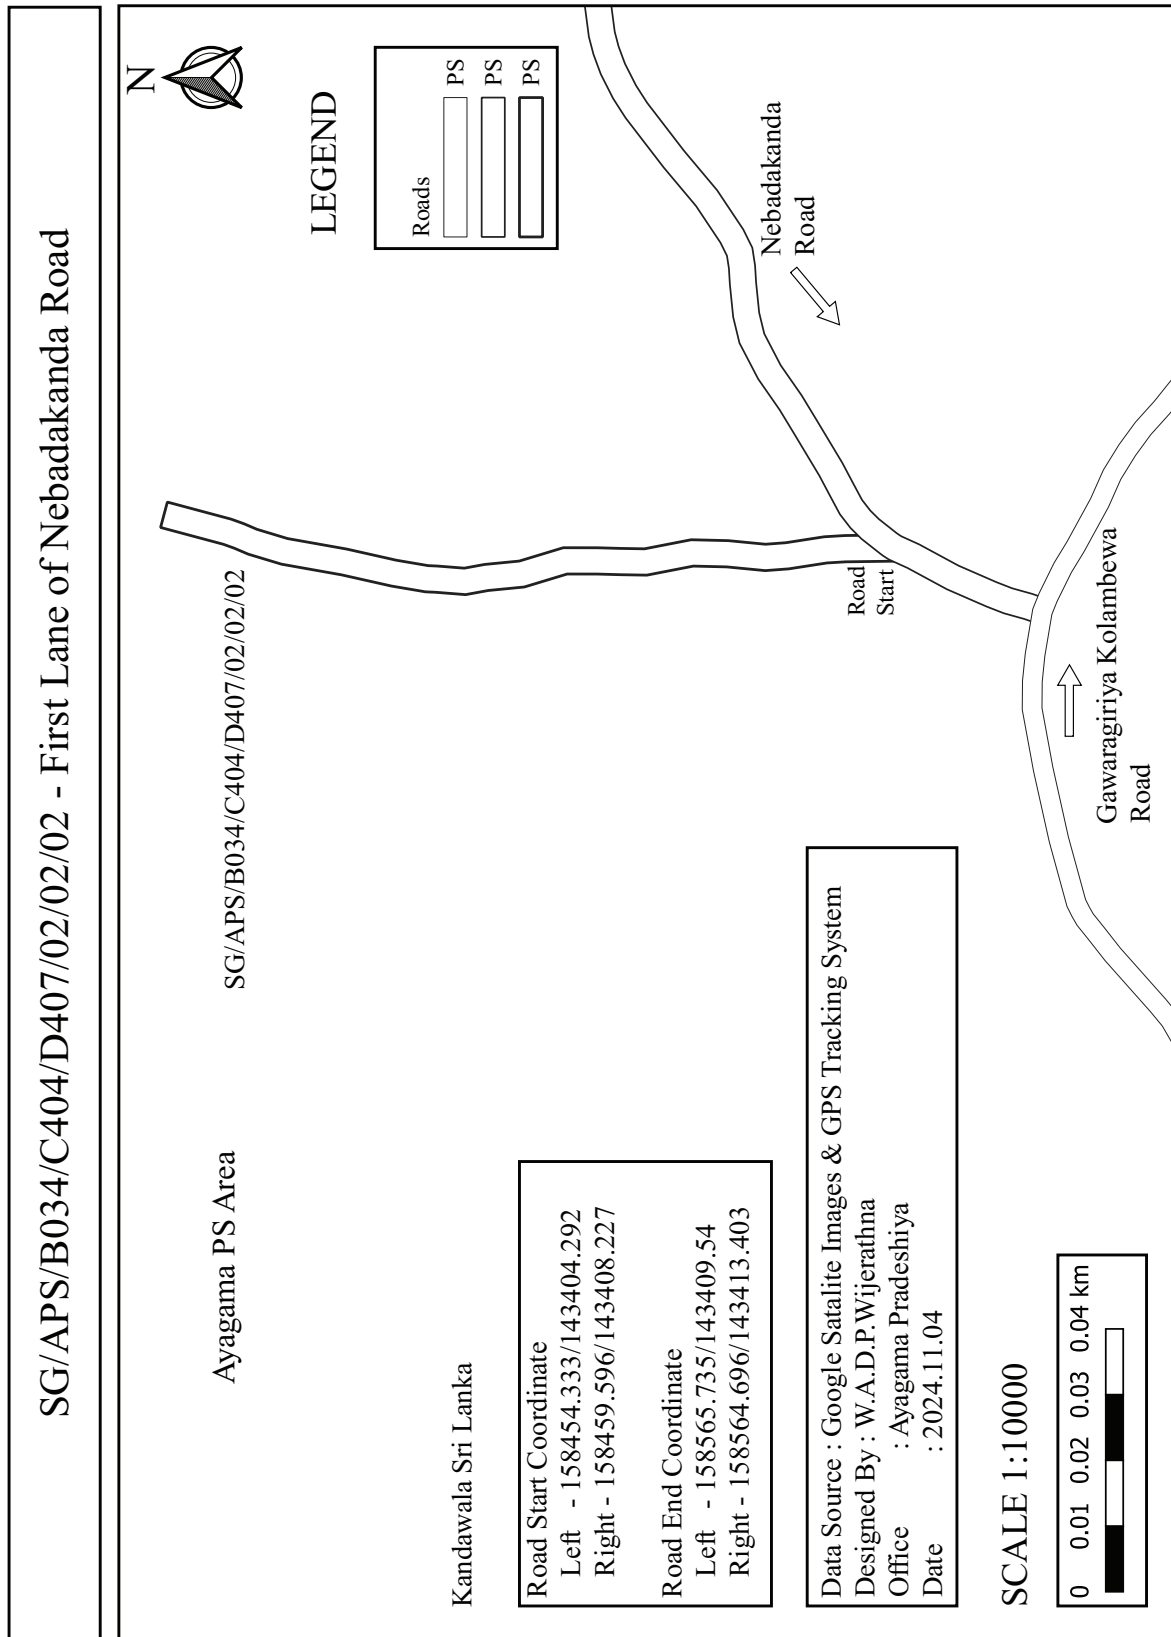



SCALE 1:10000


0 0.01 0.02 0.03 0.04 km


N

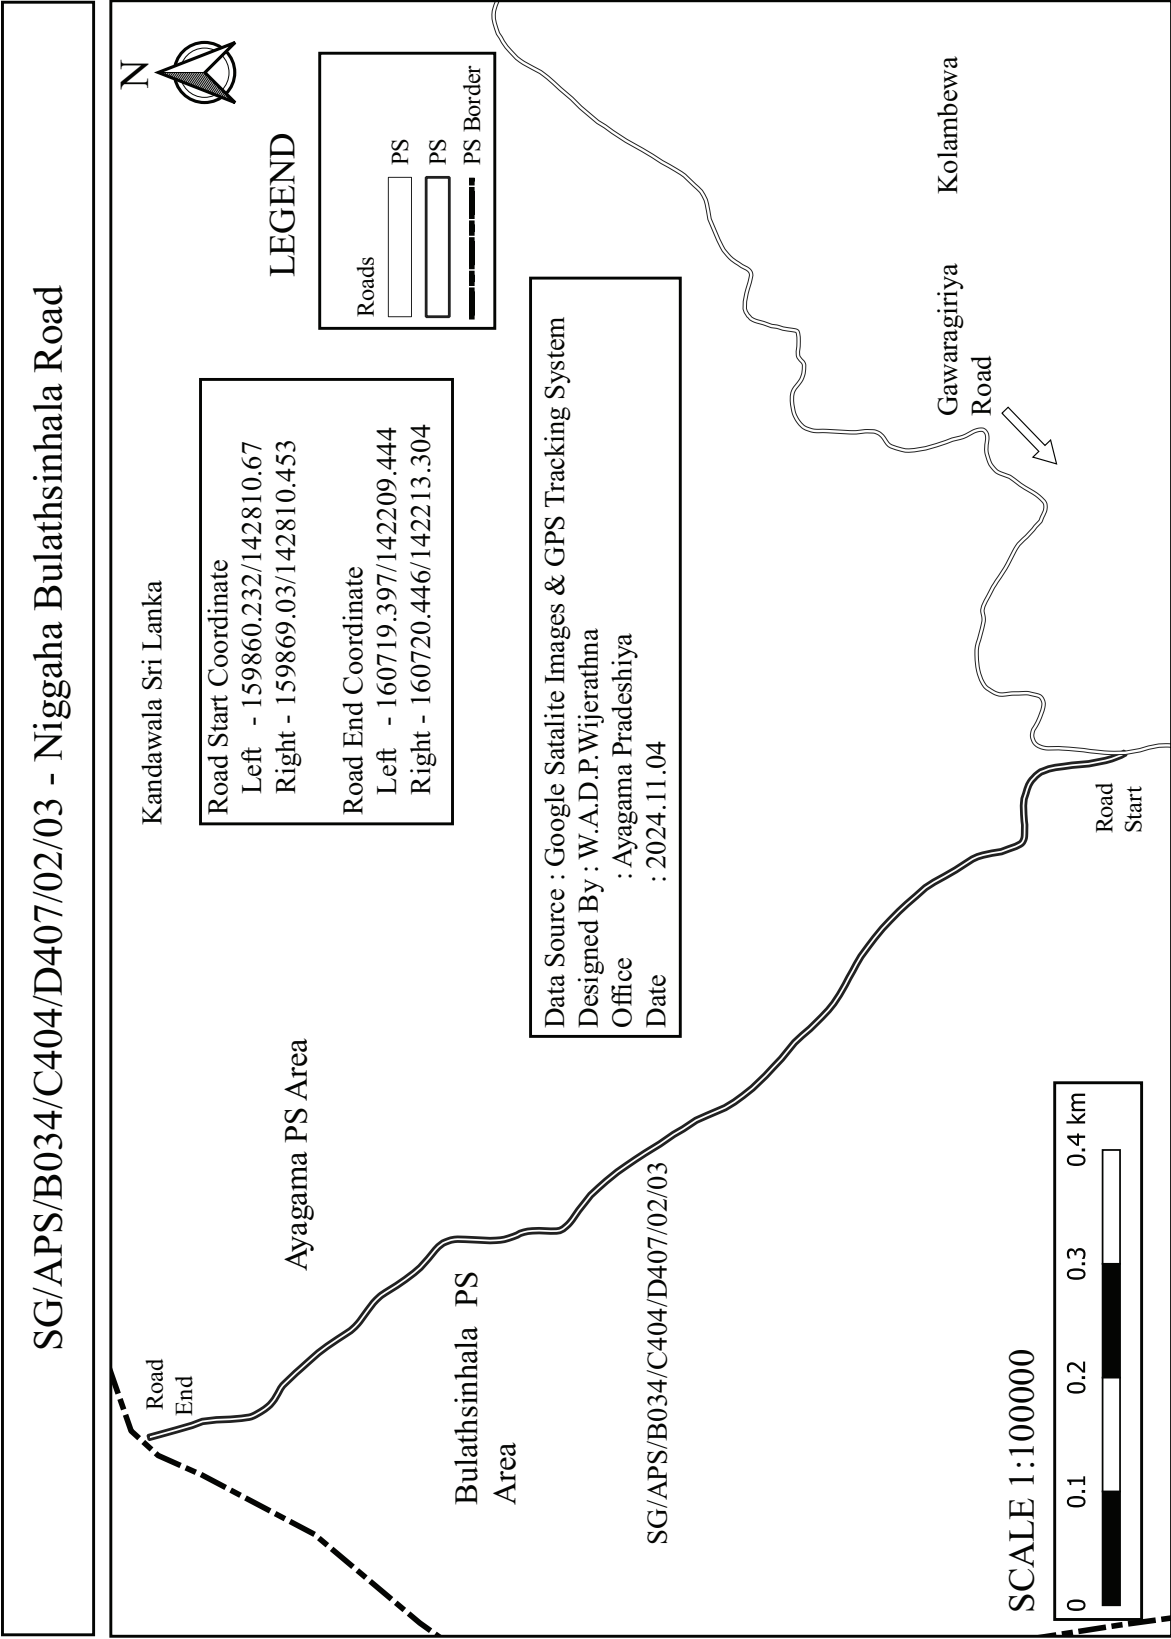


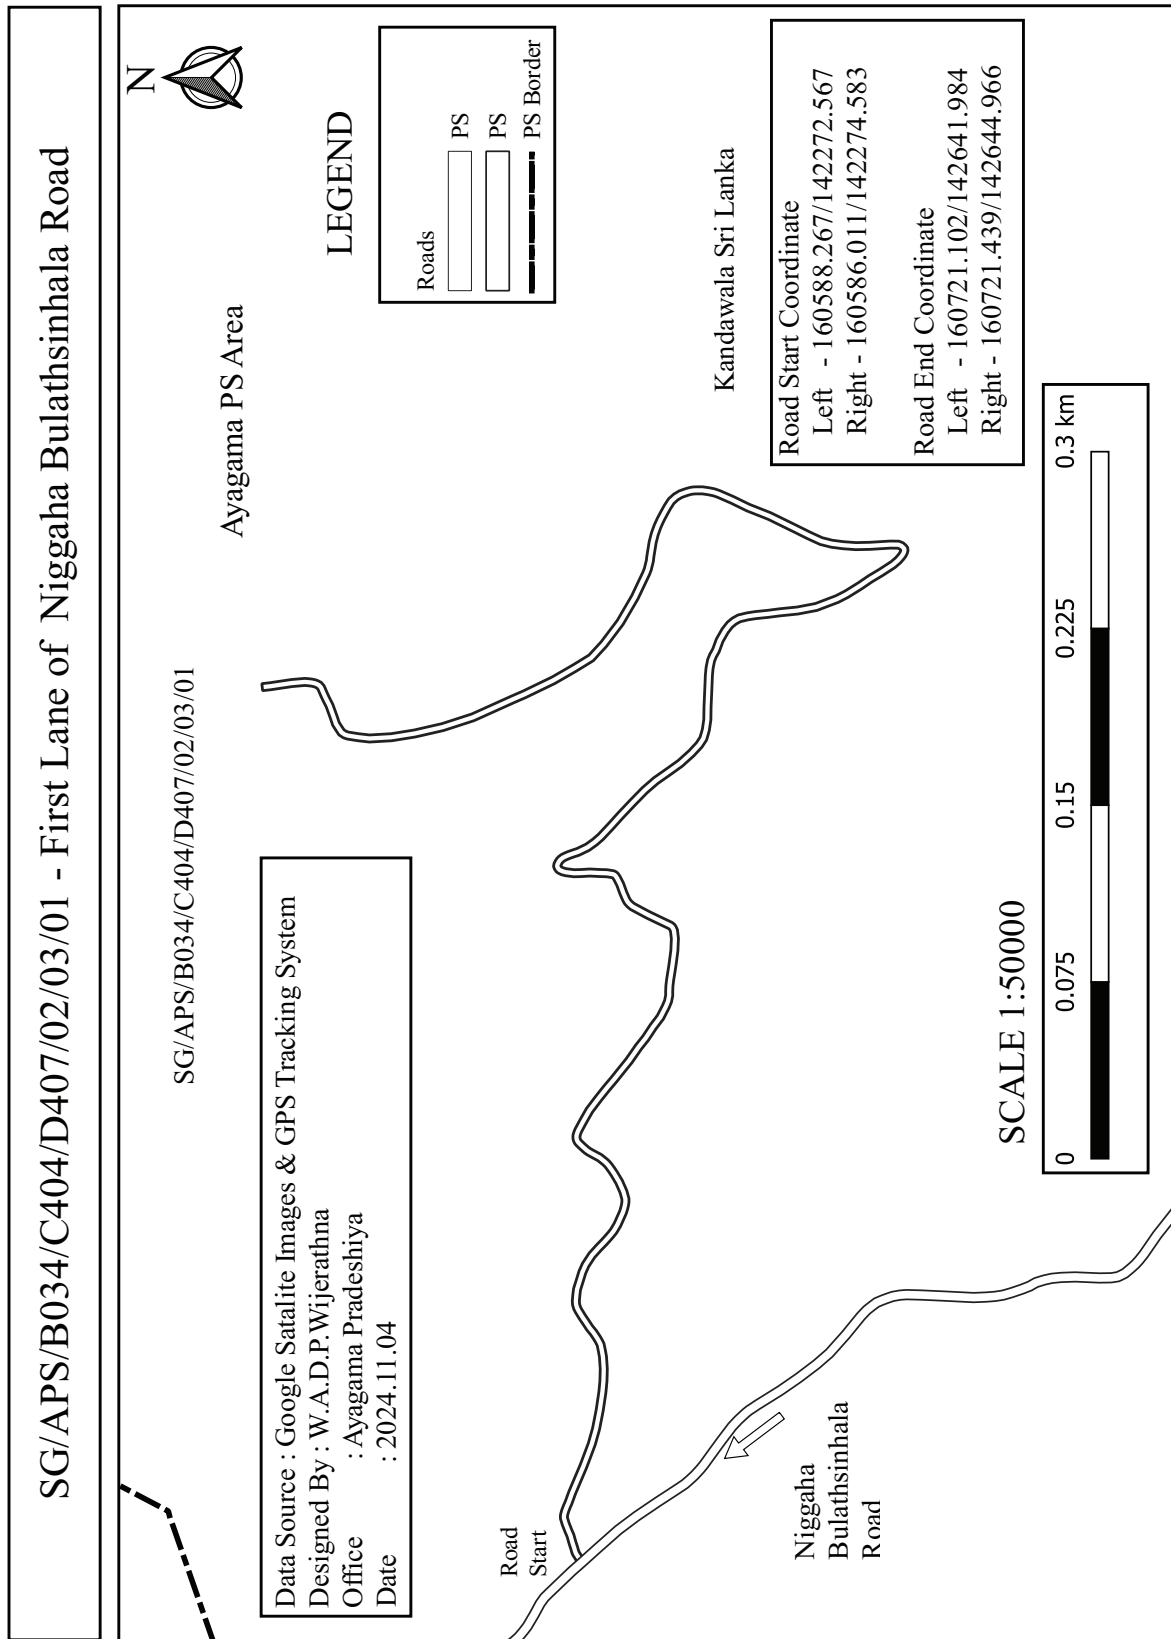


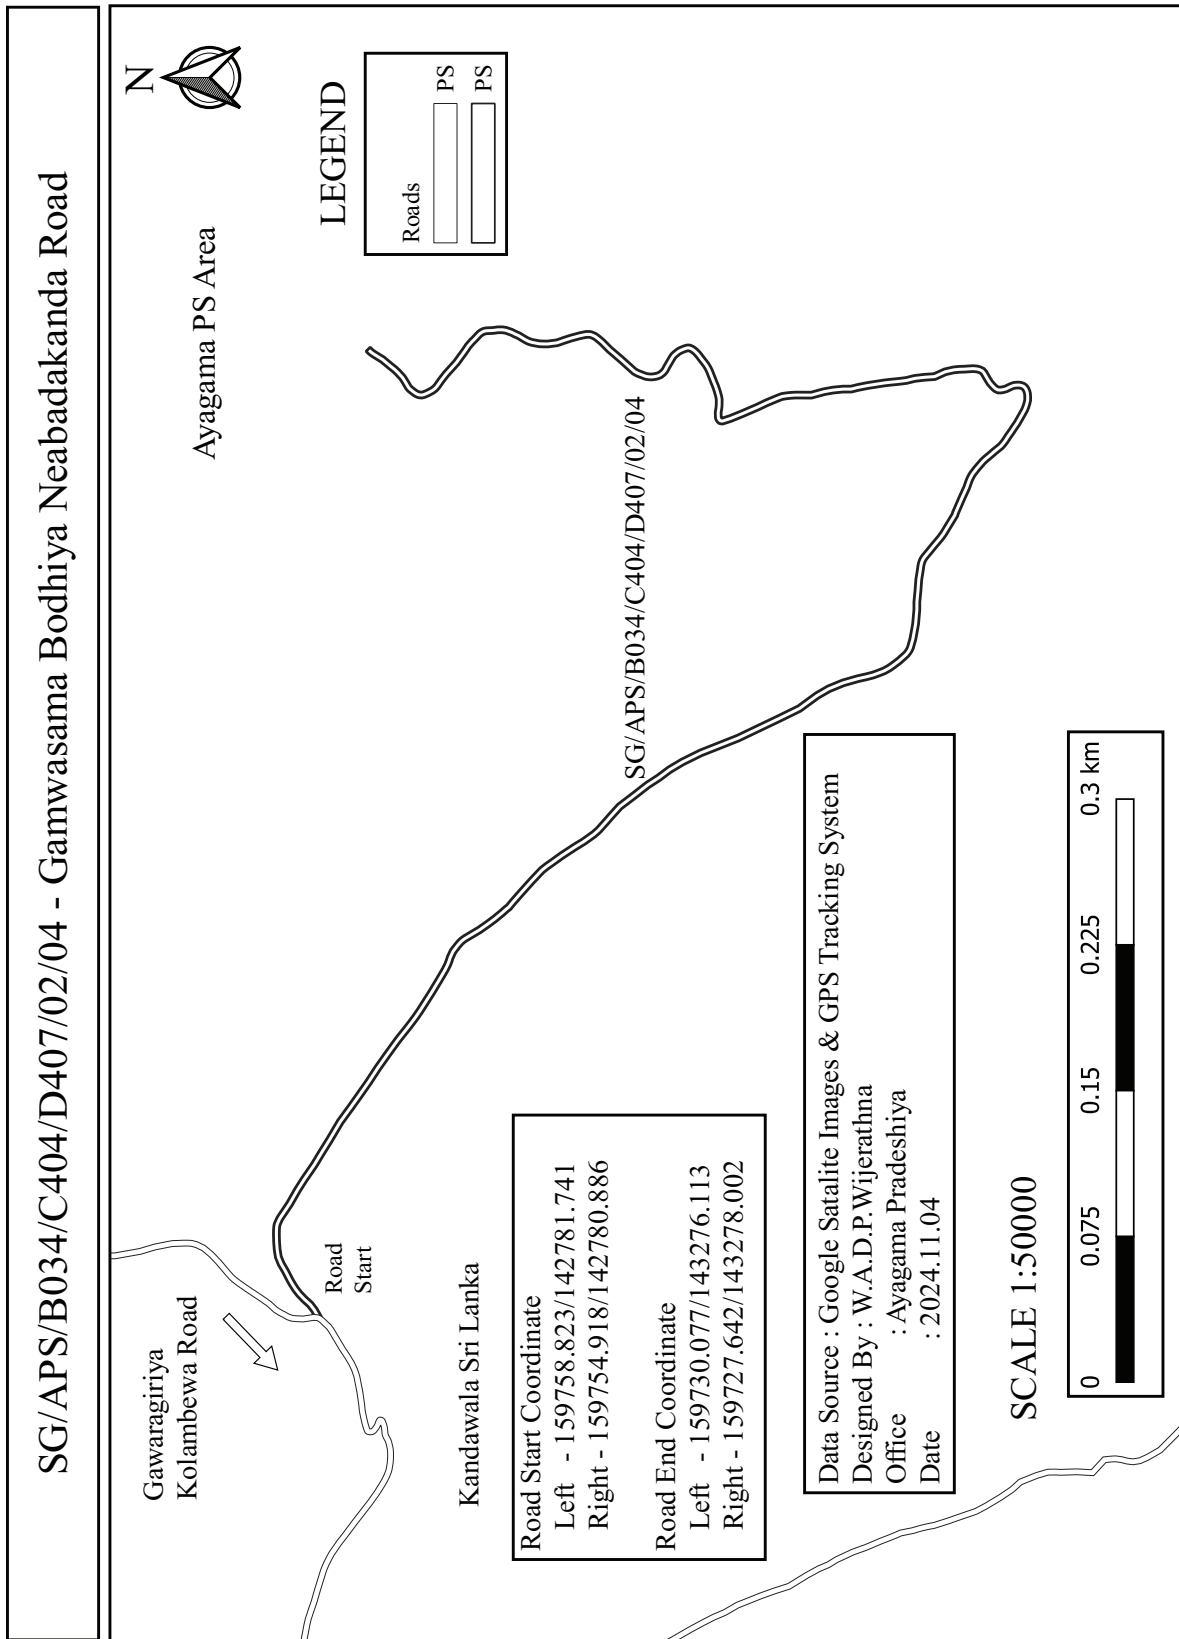


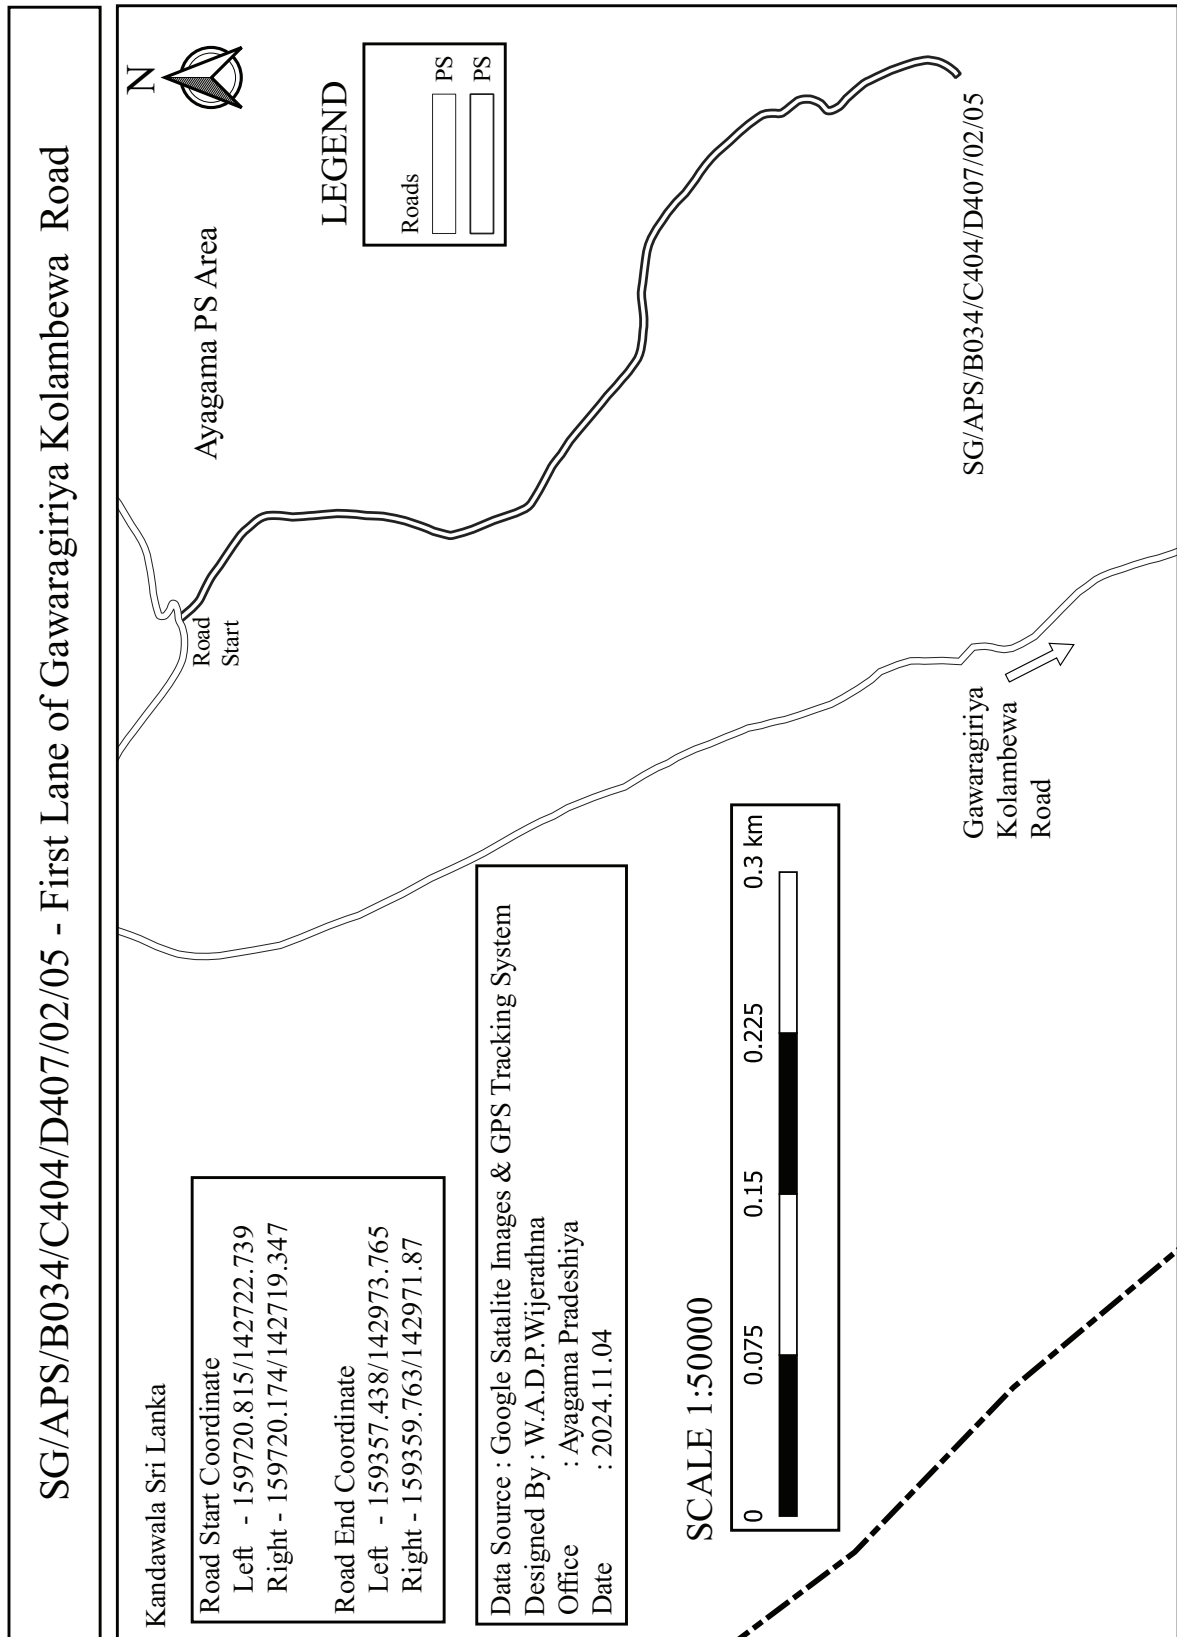


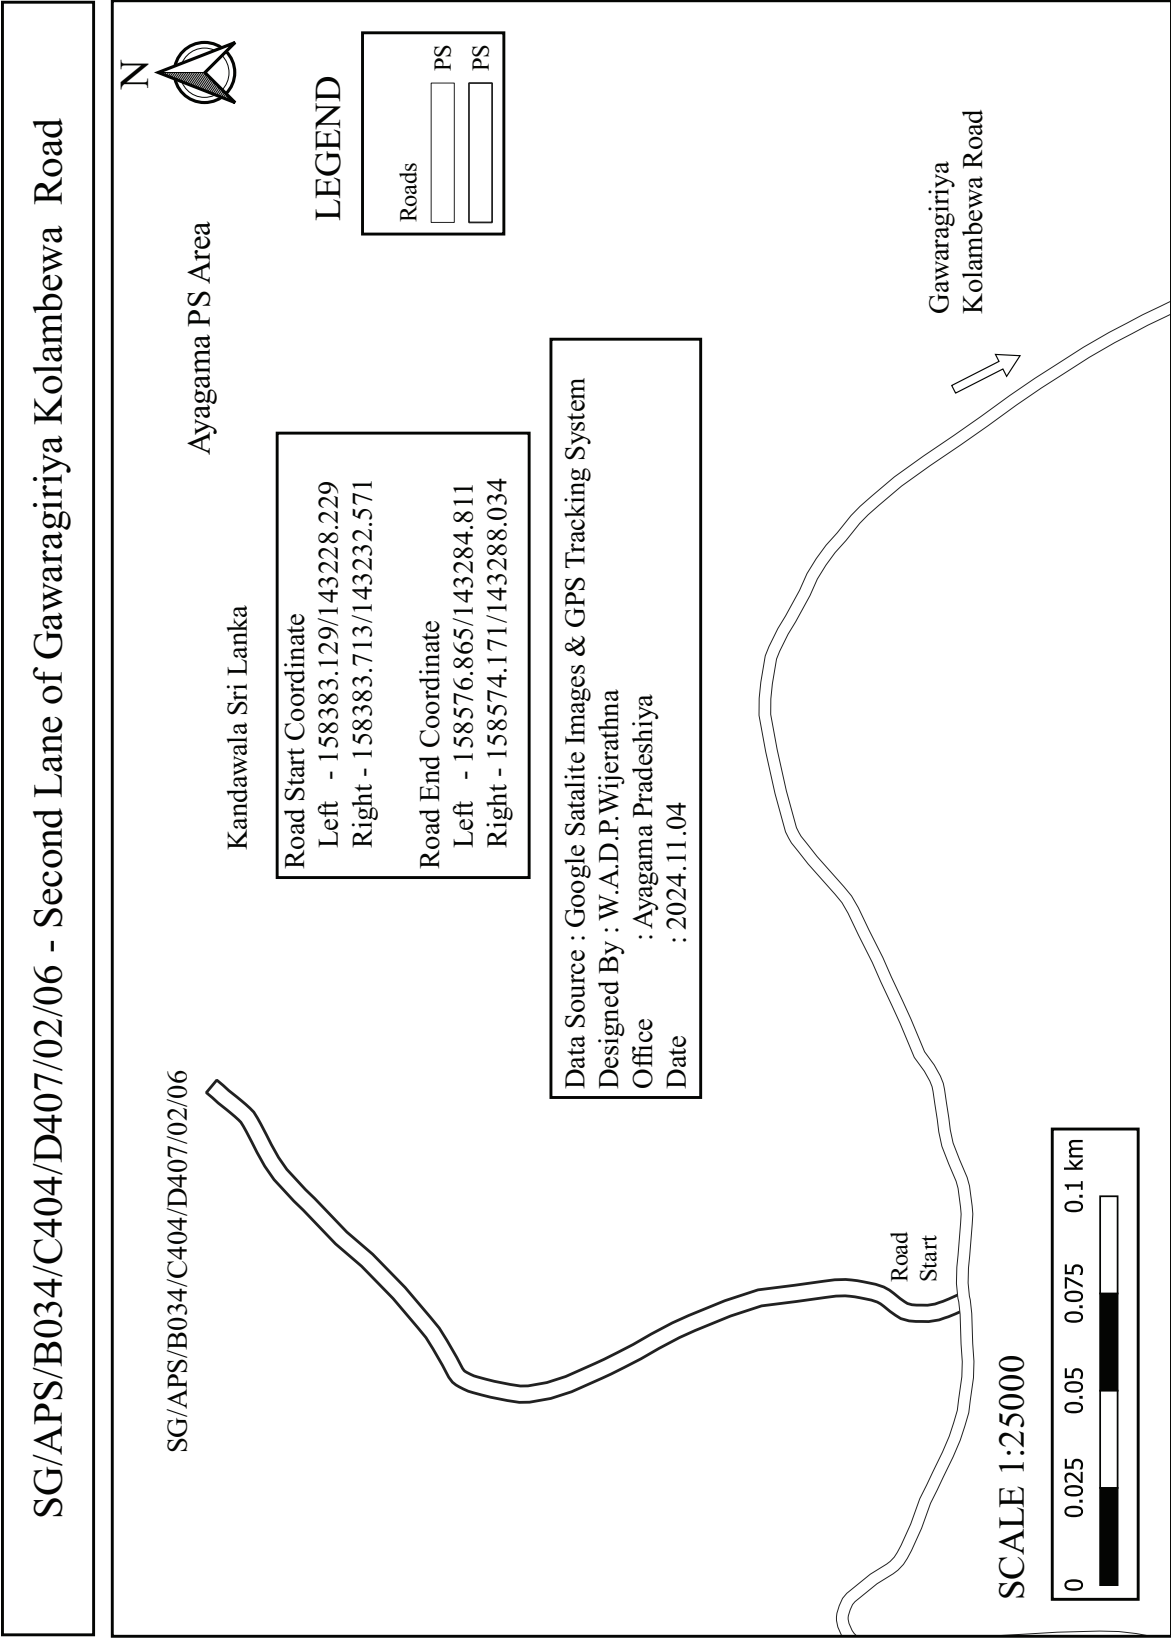


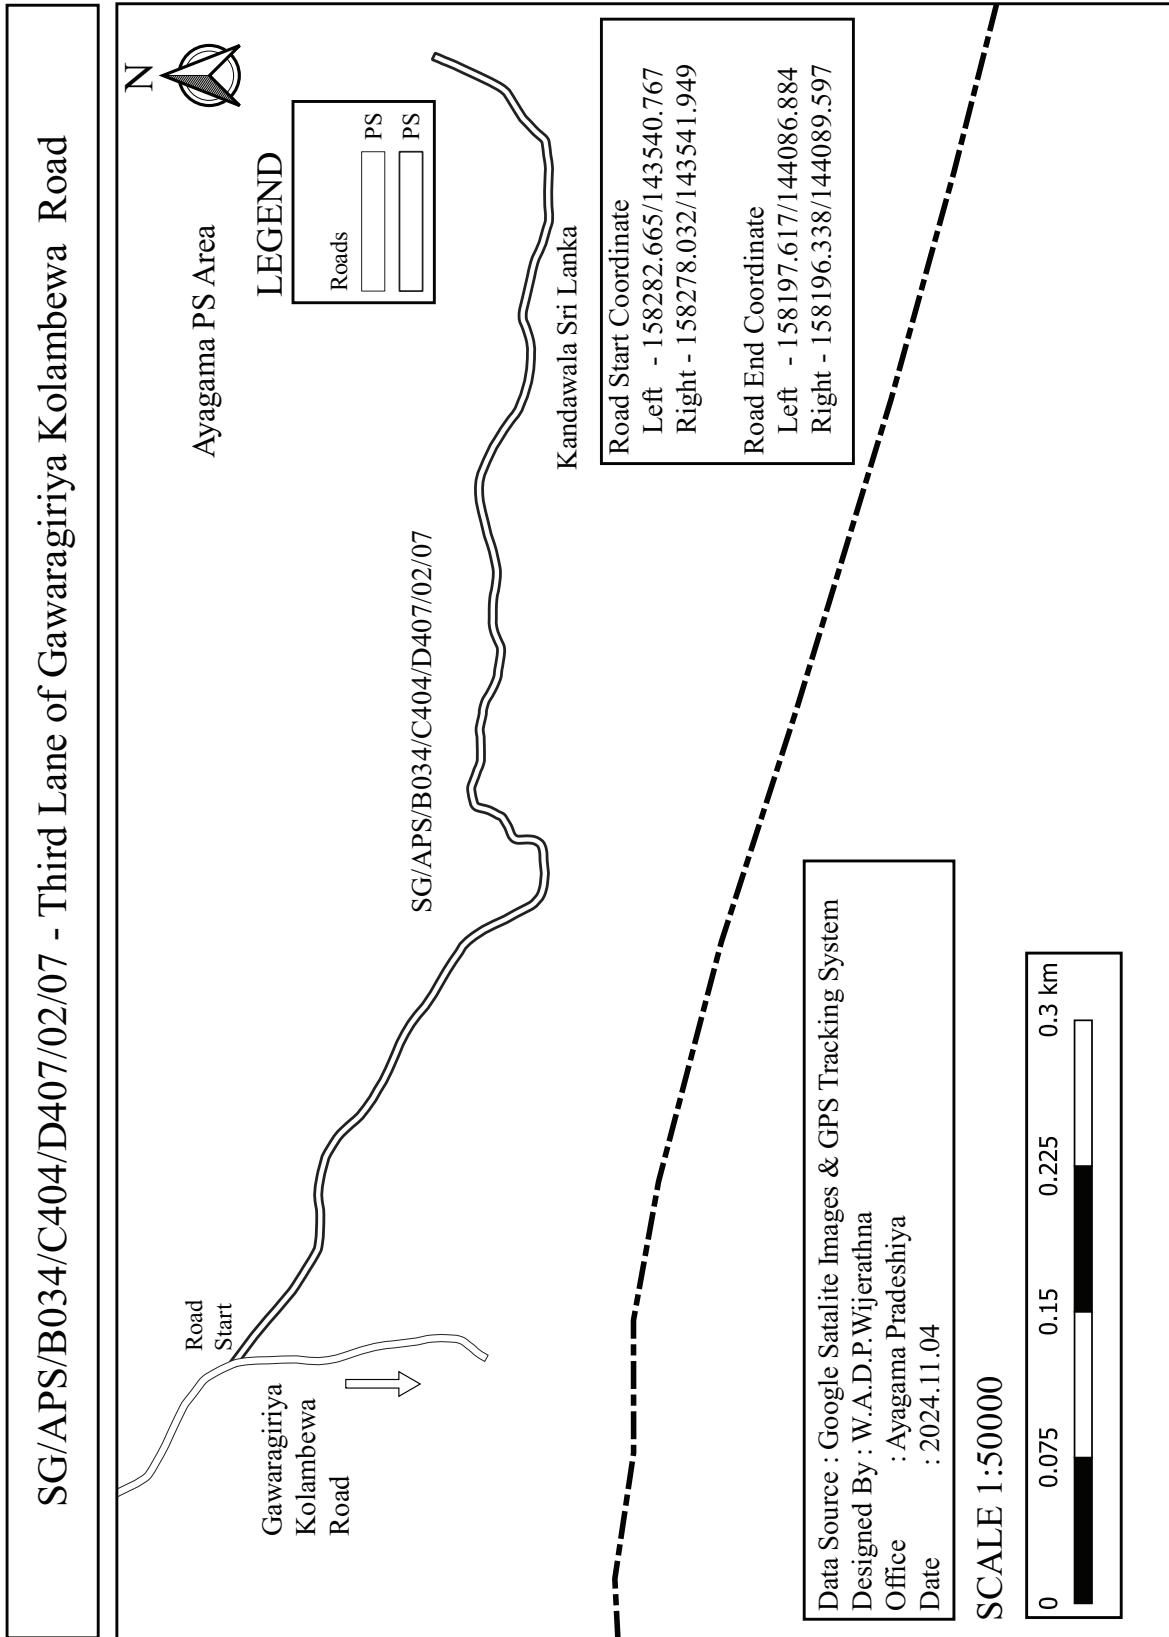


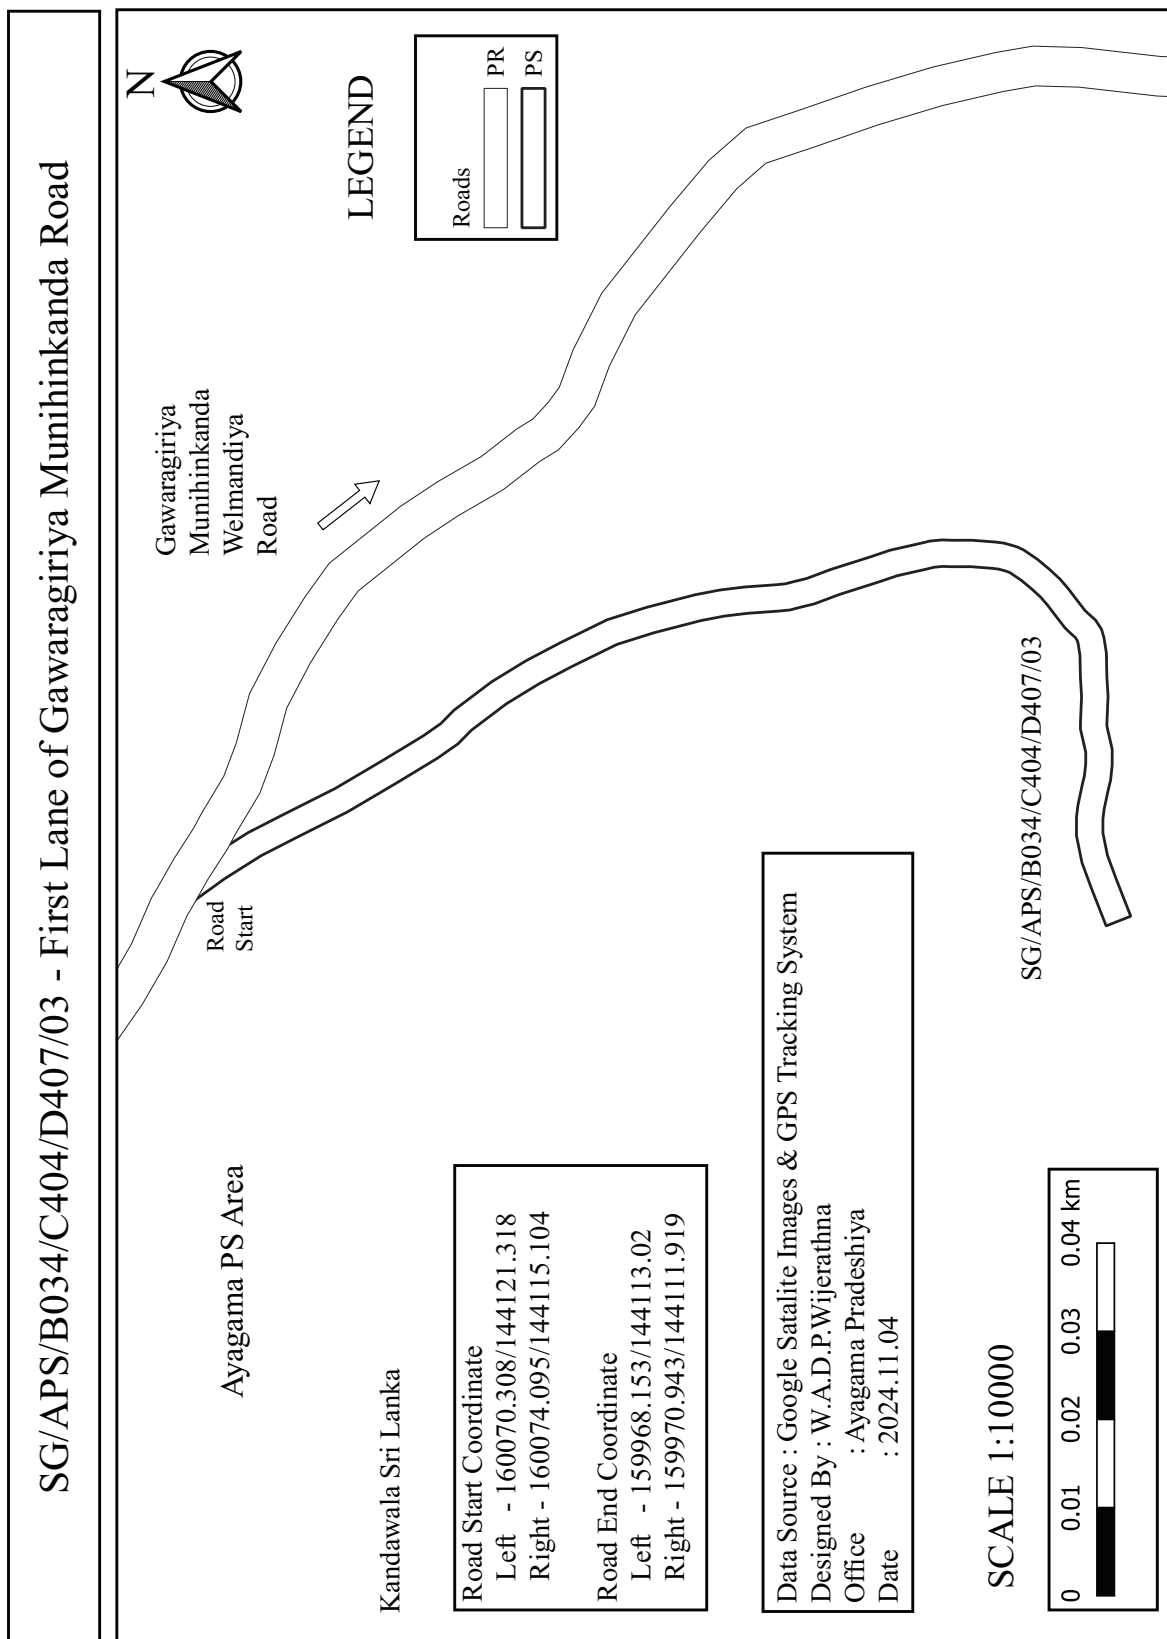


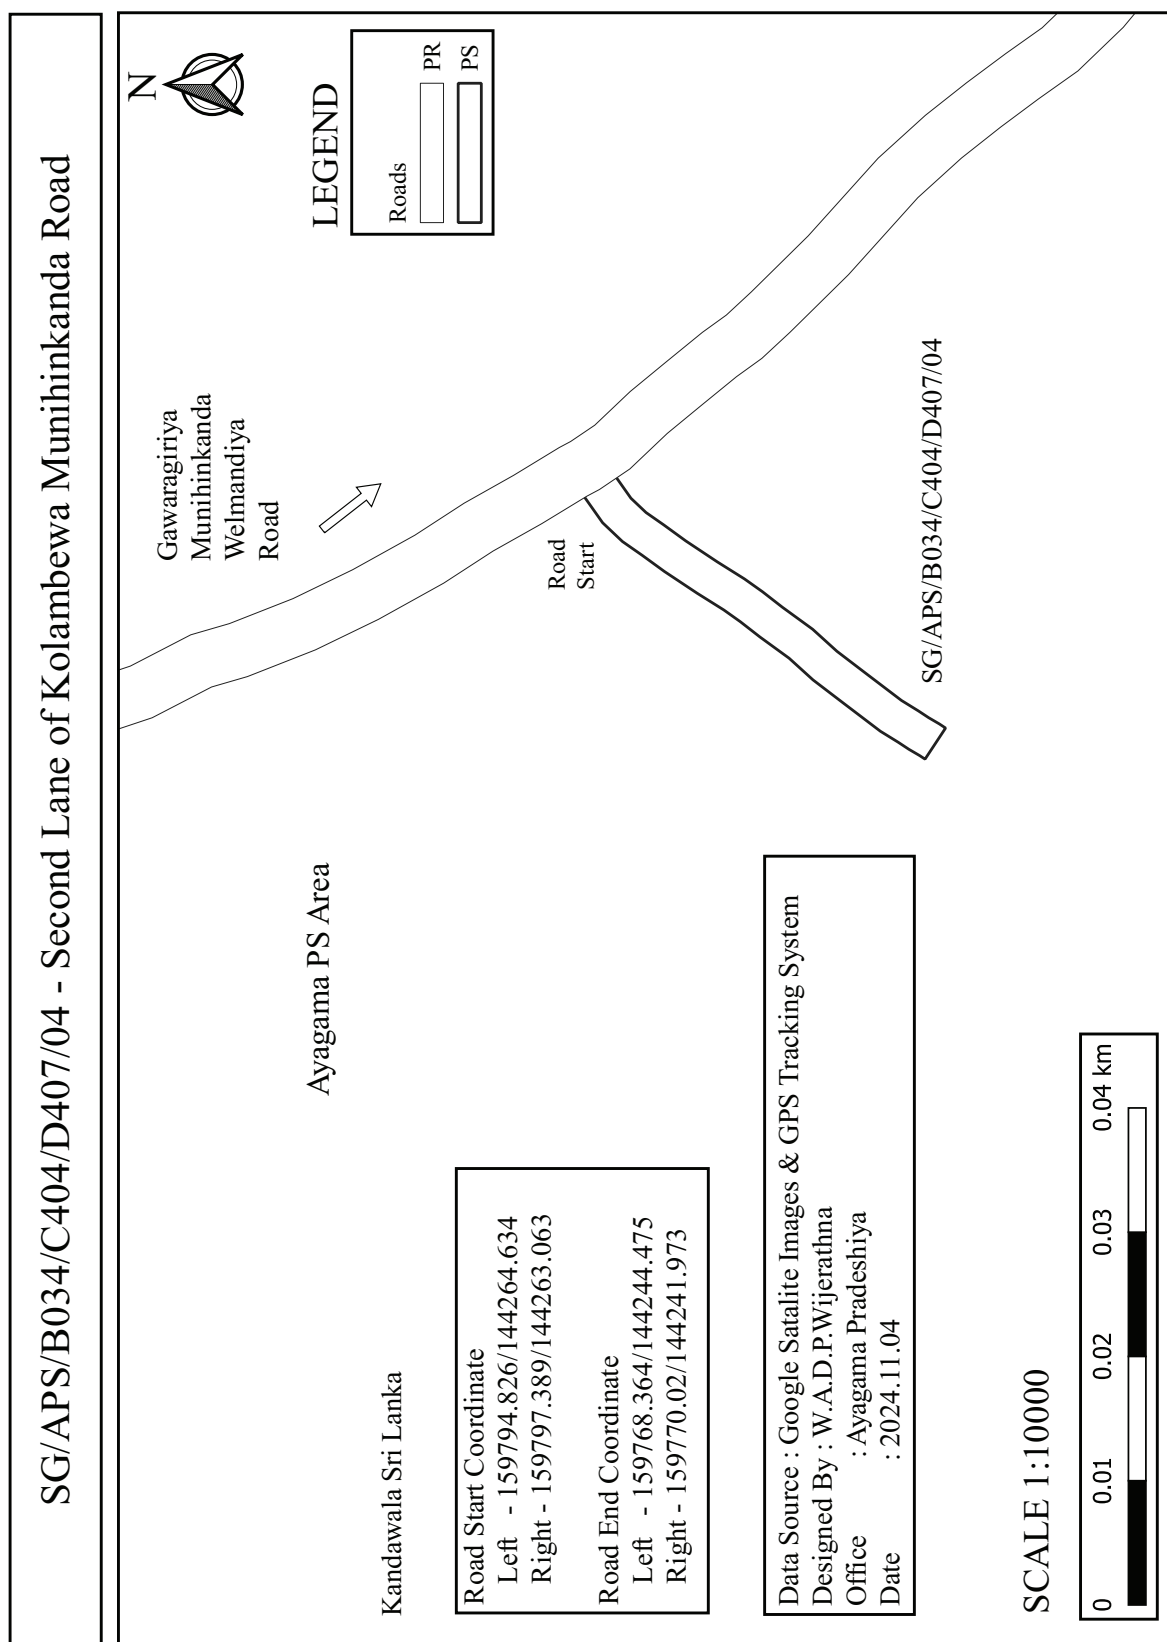


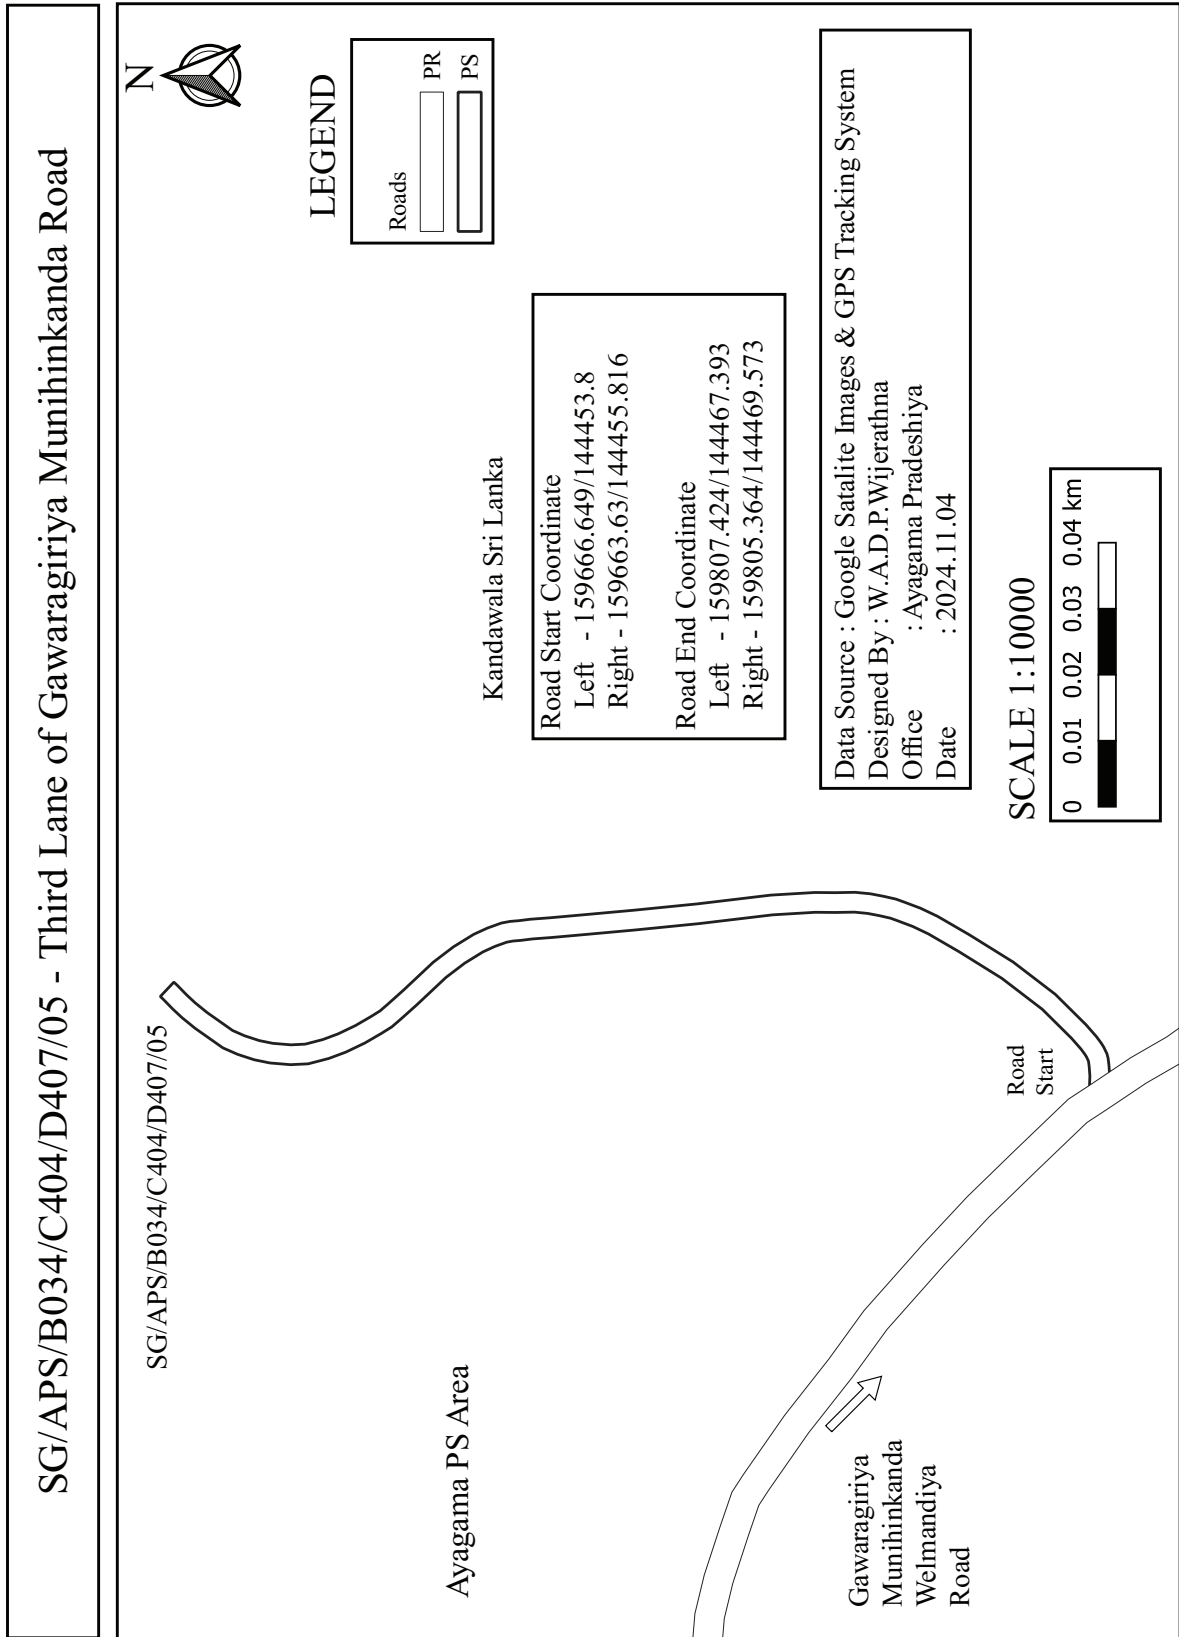


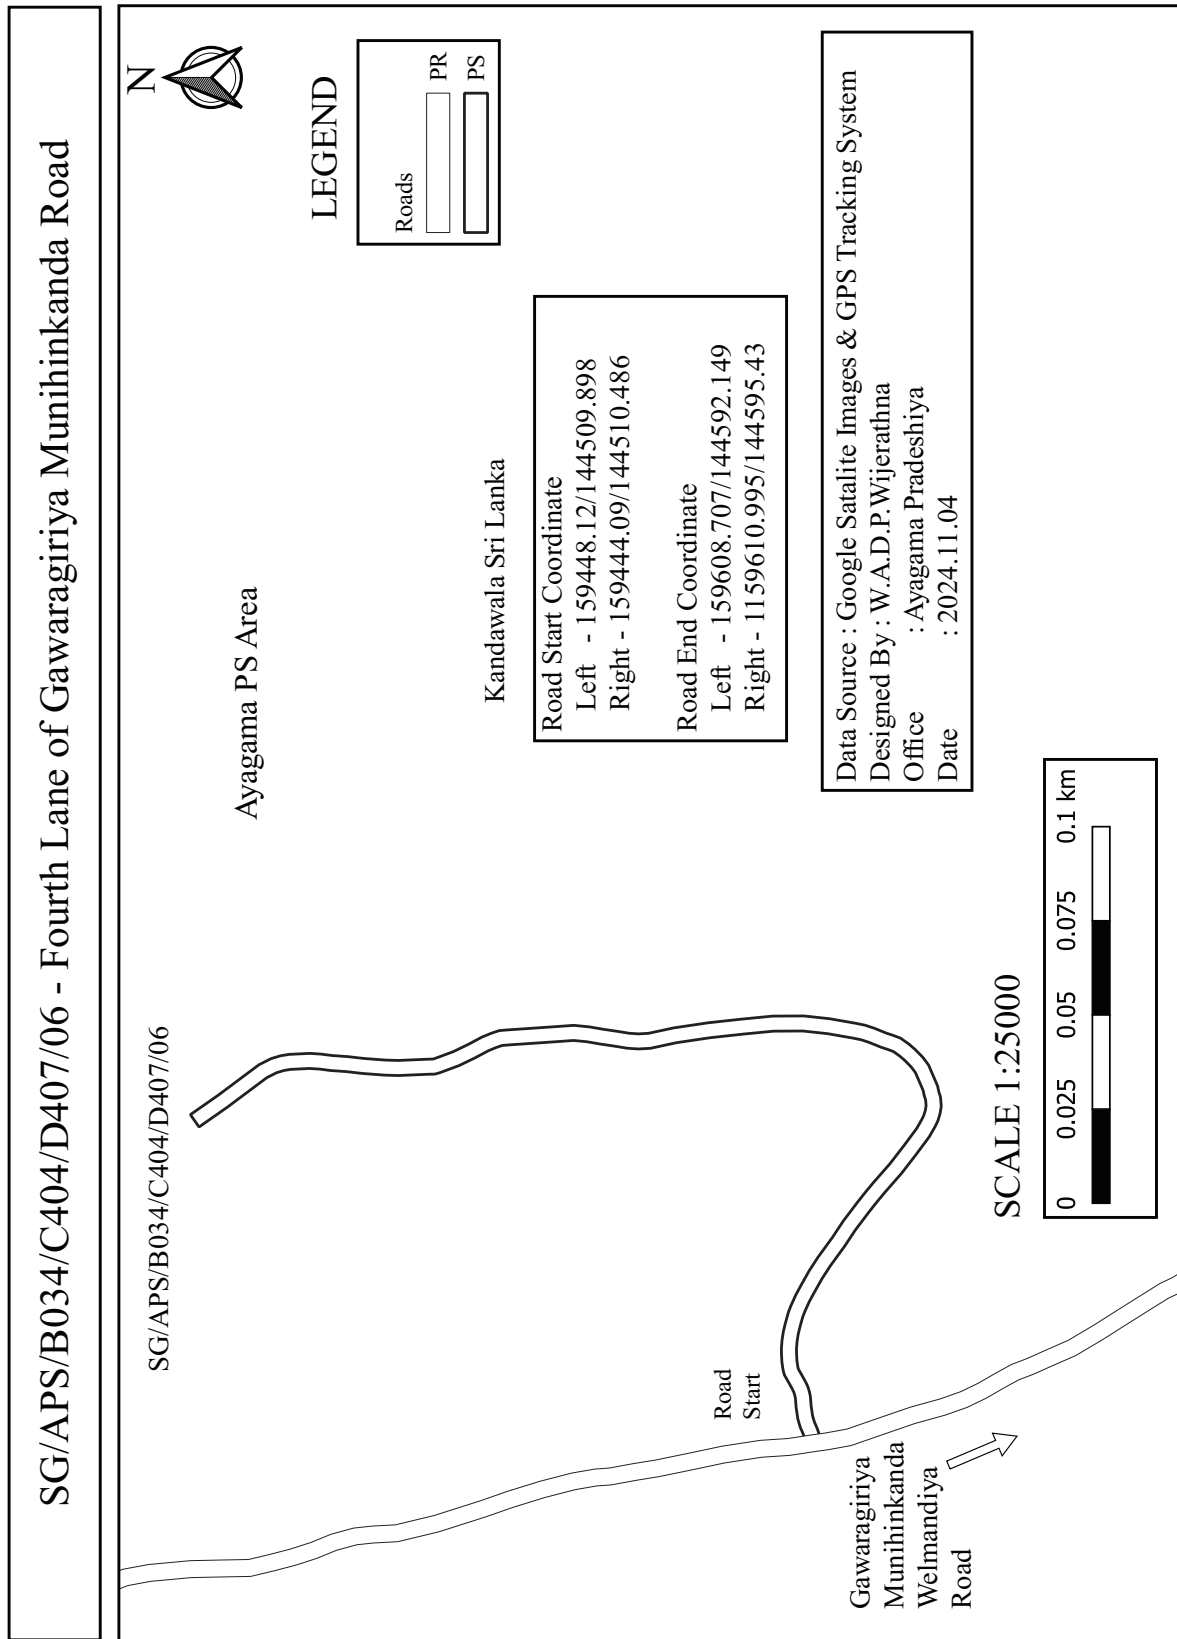


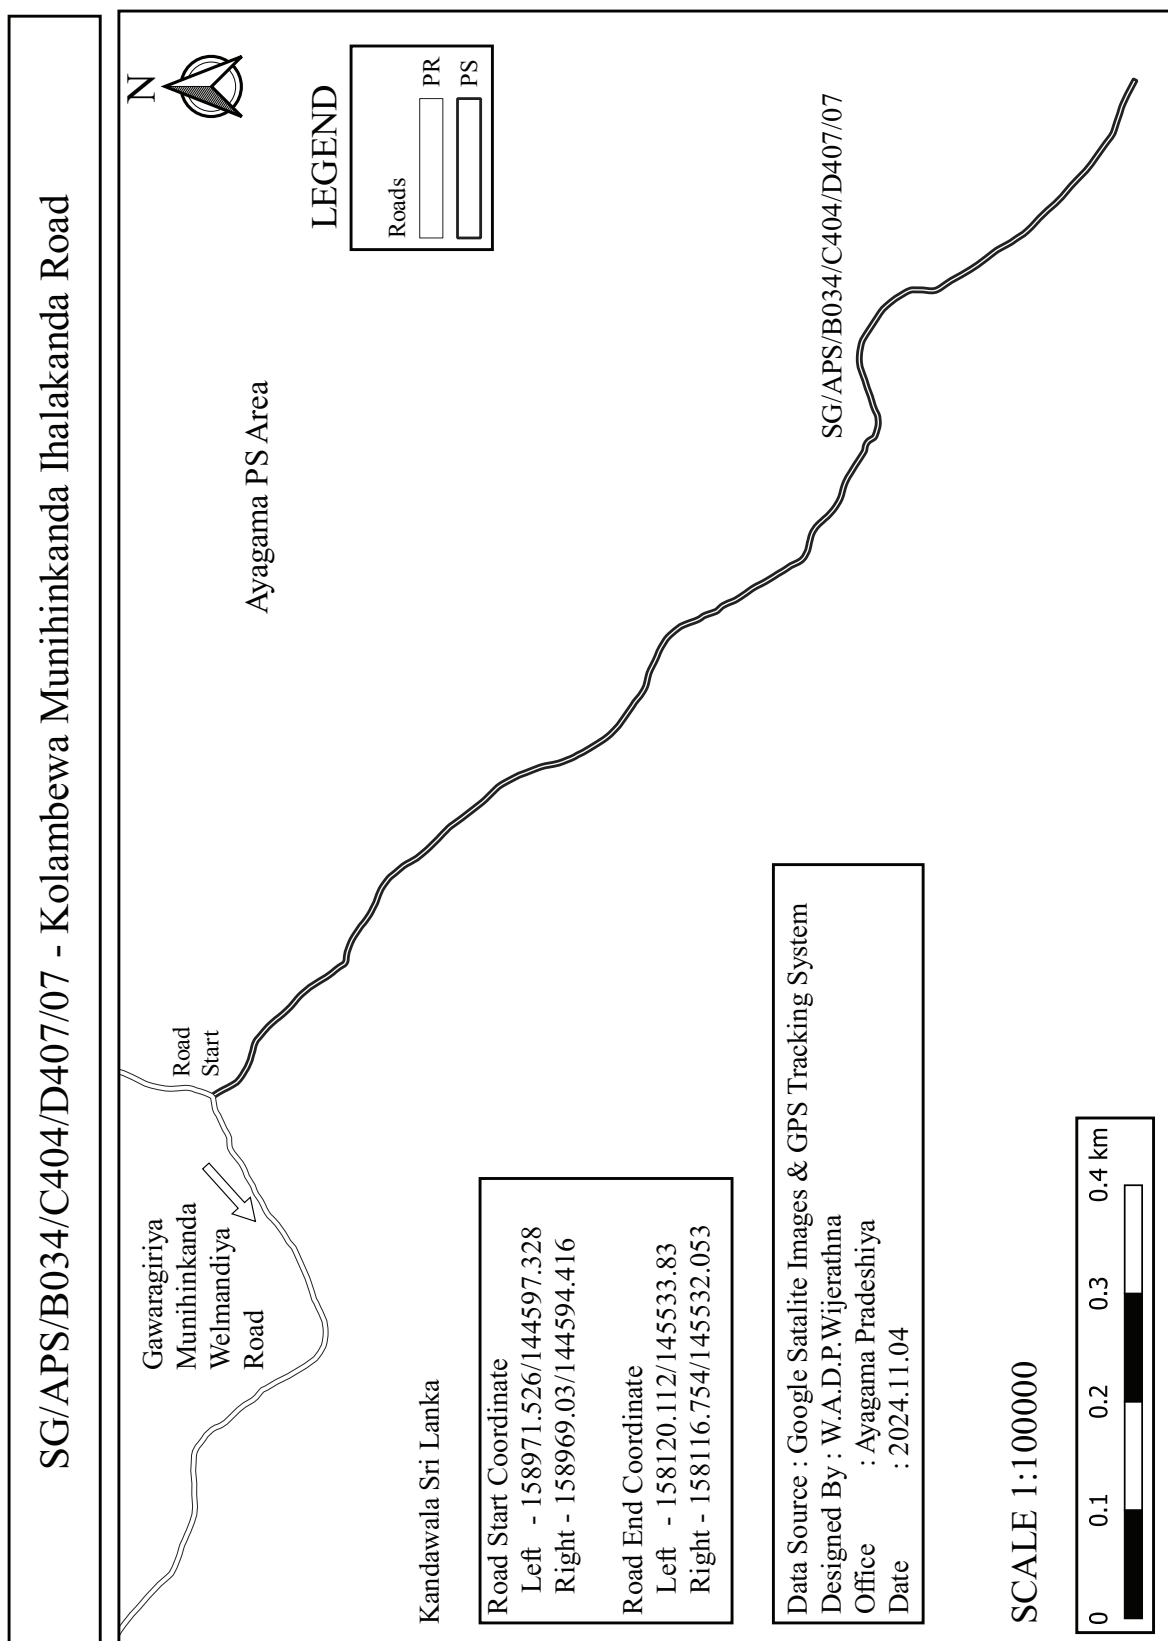


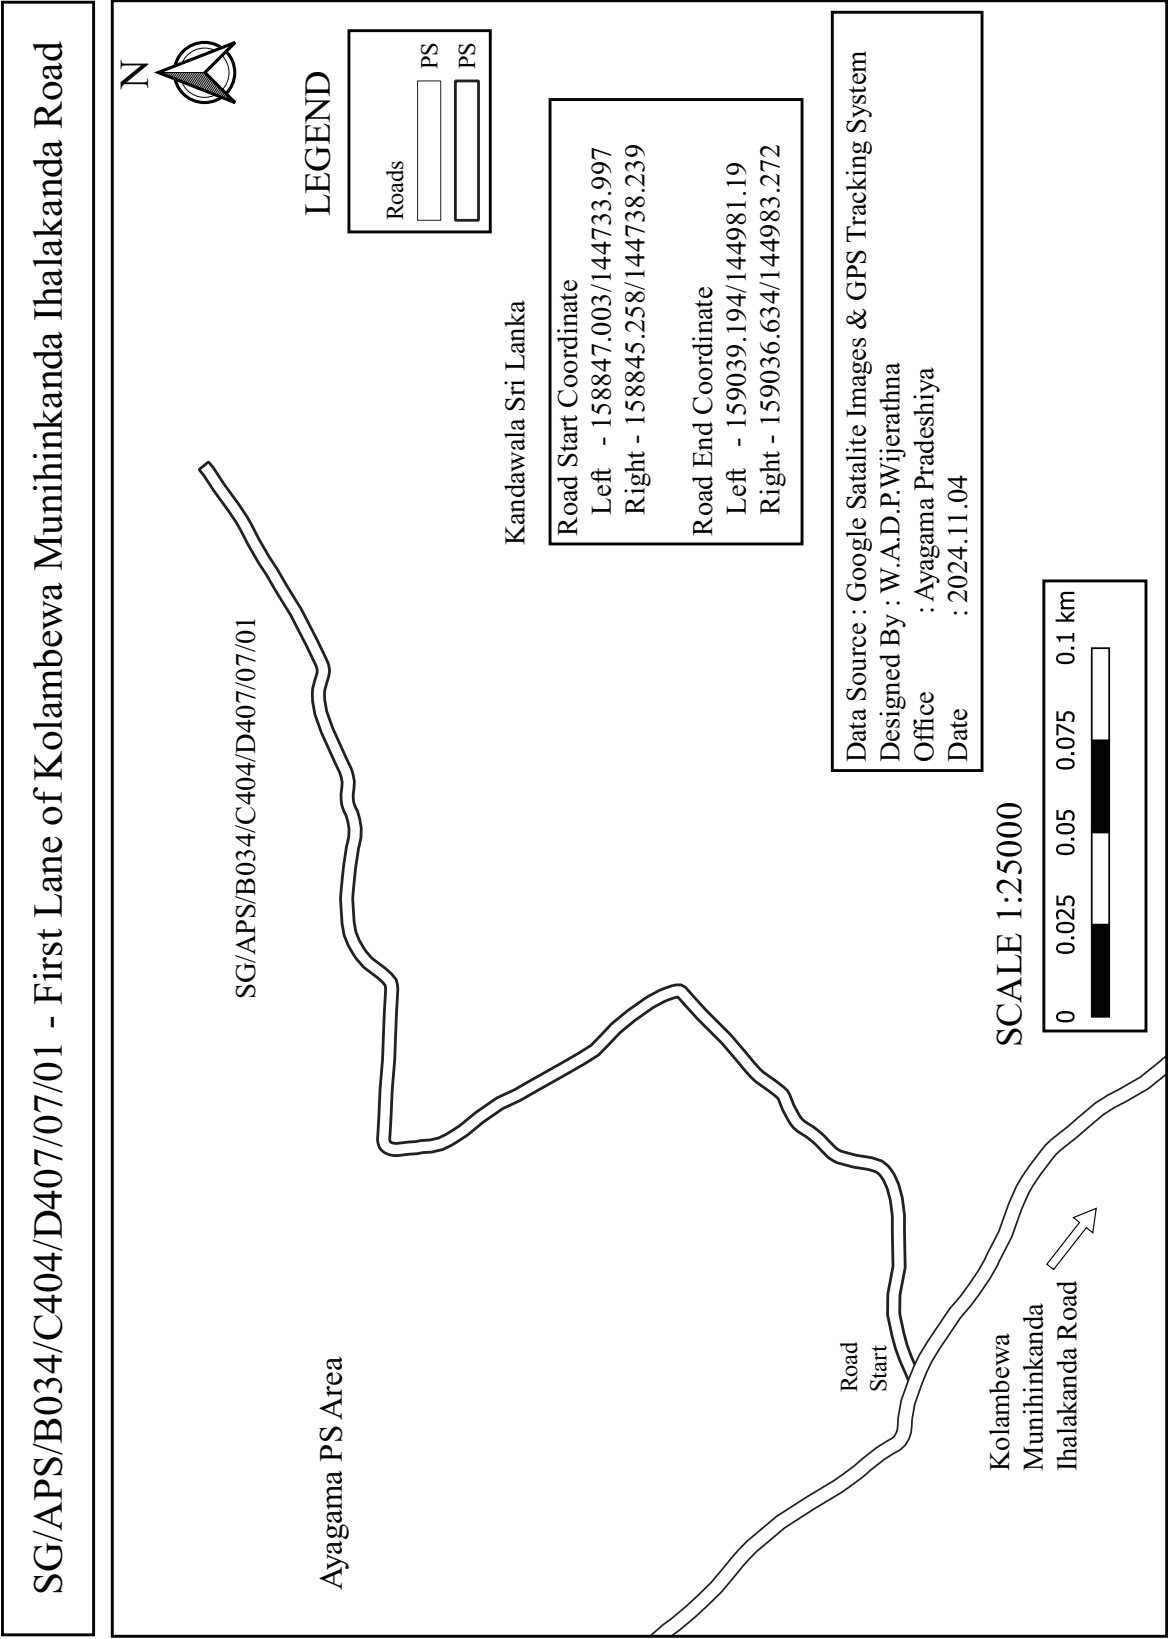


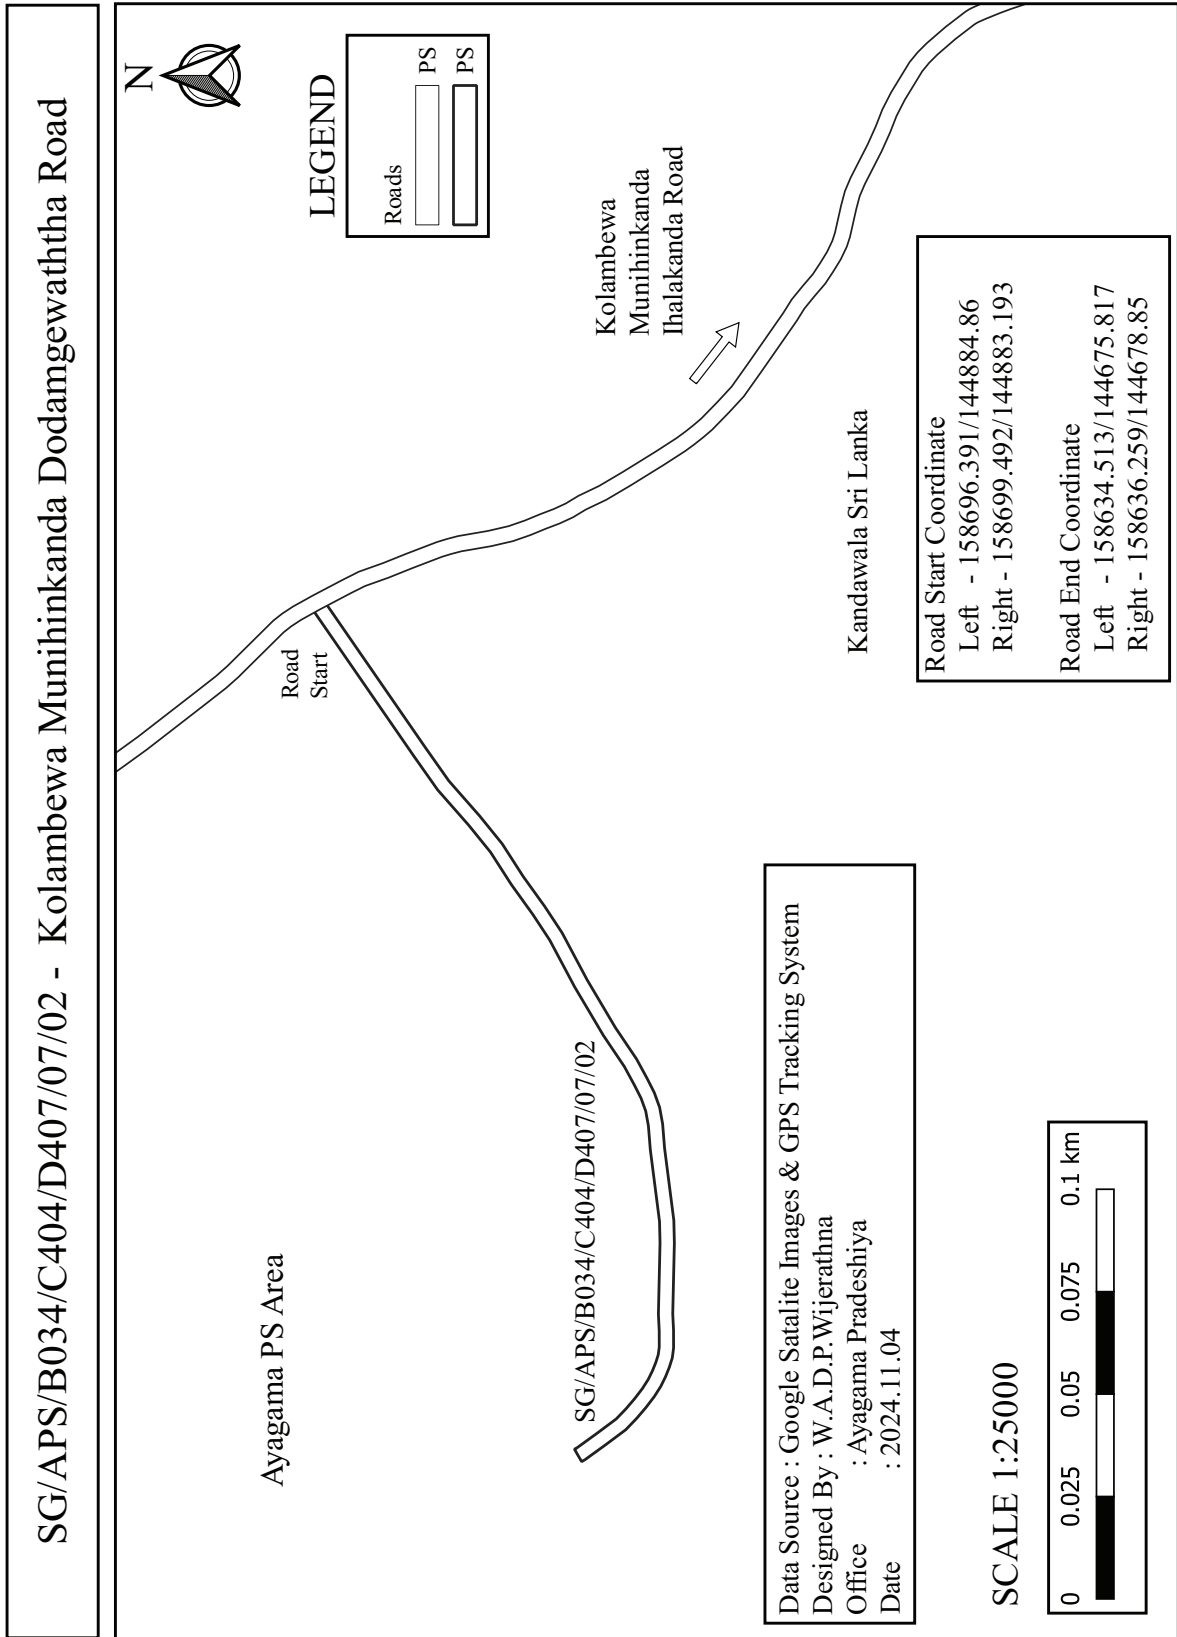


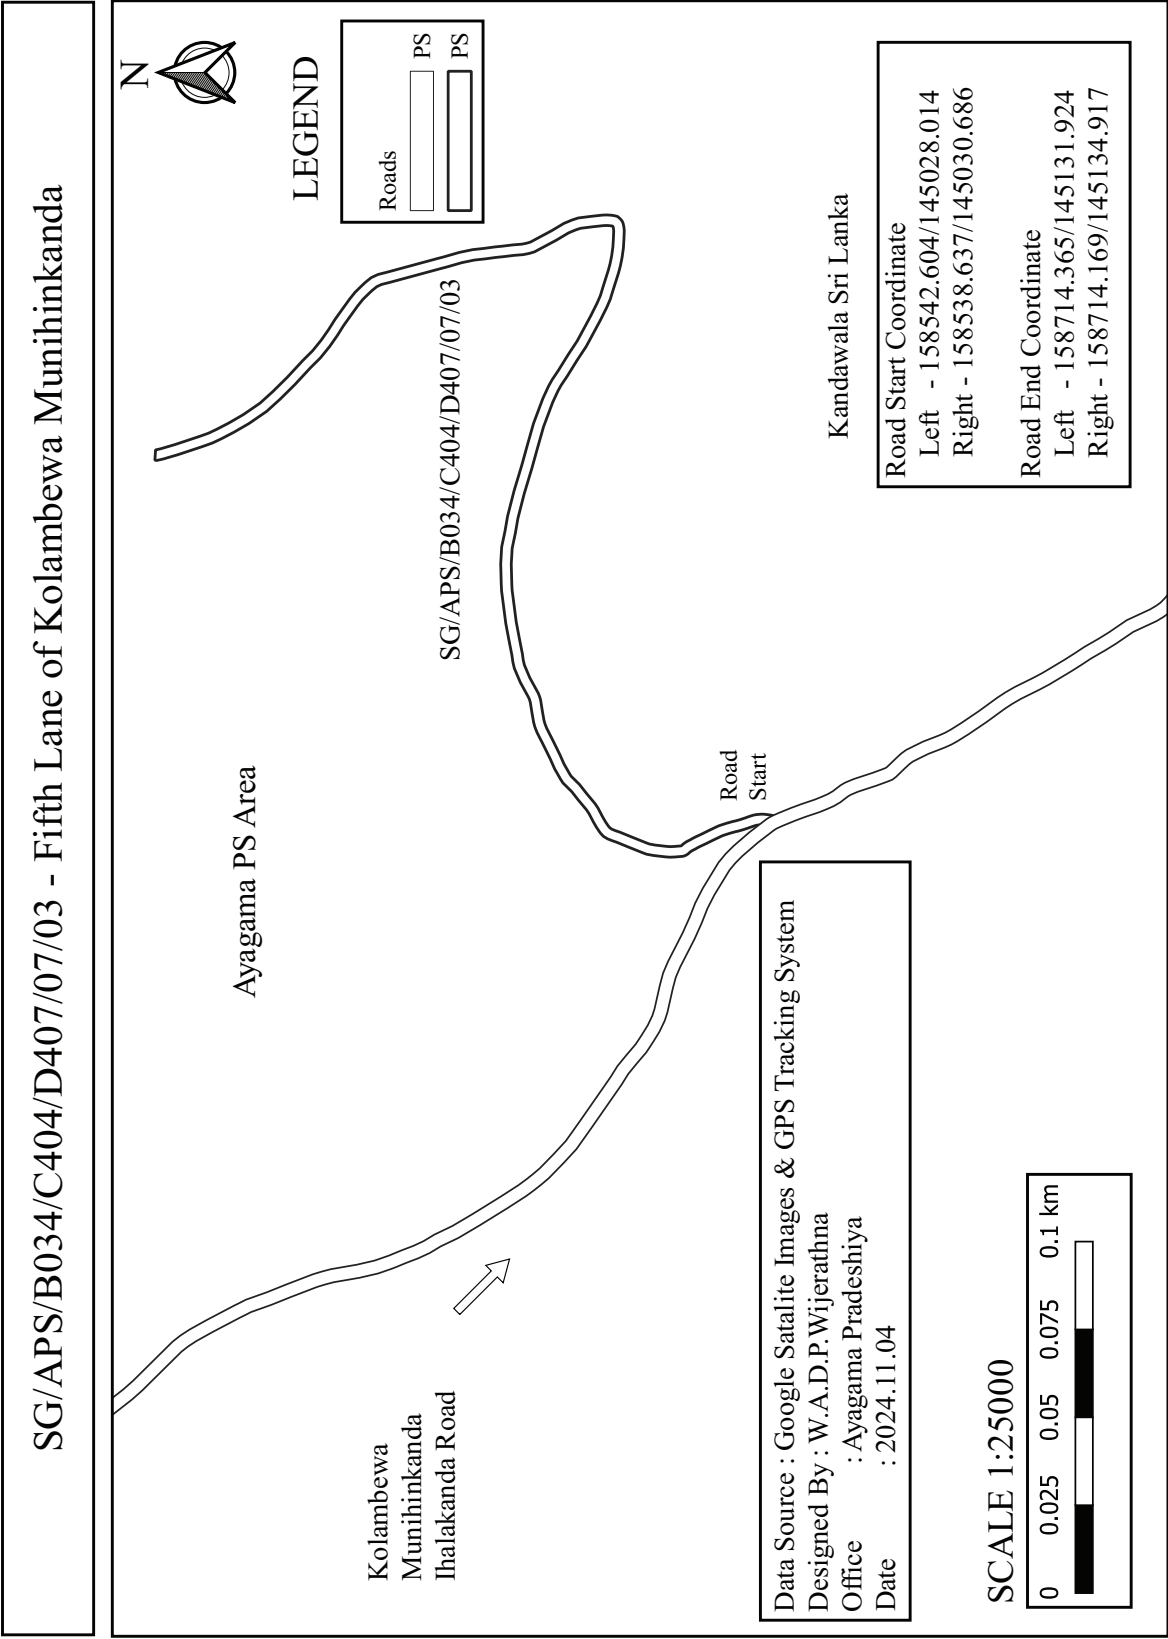


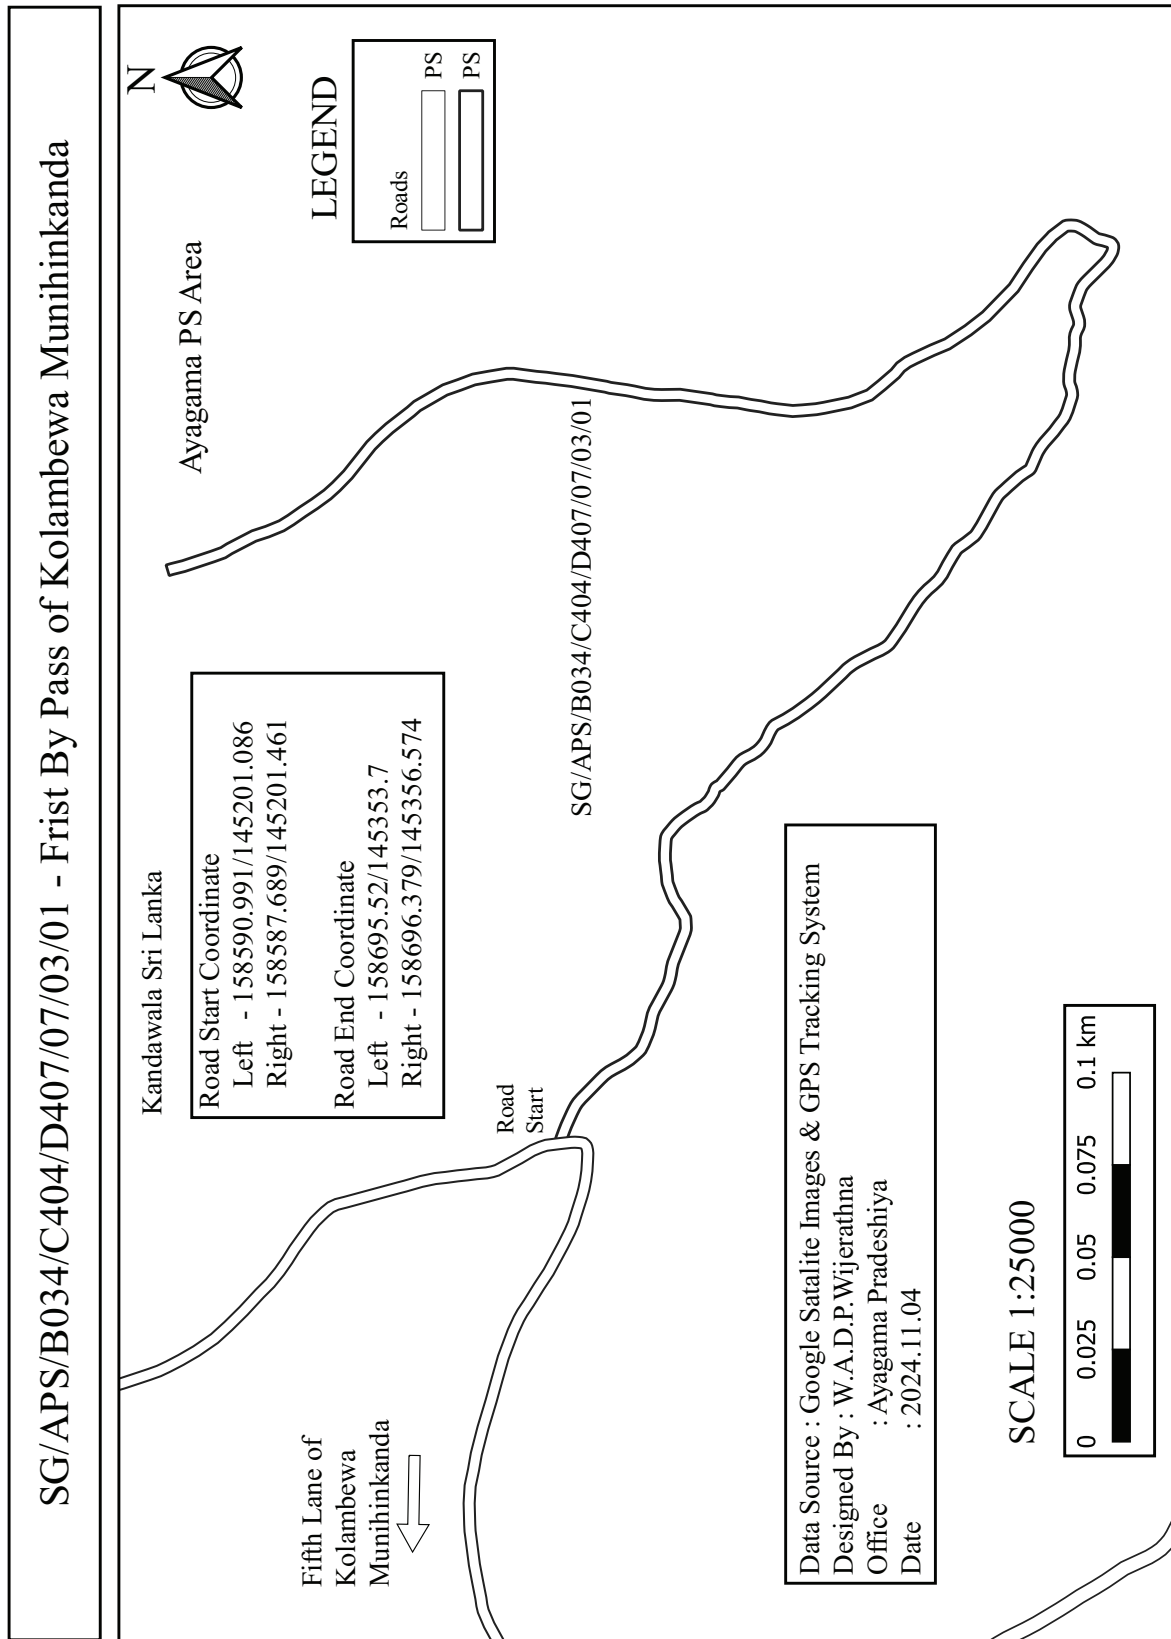


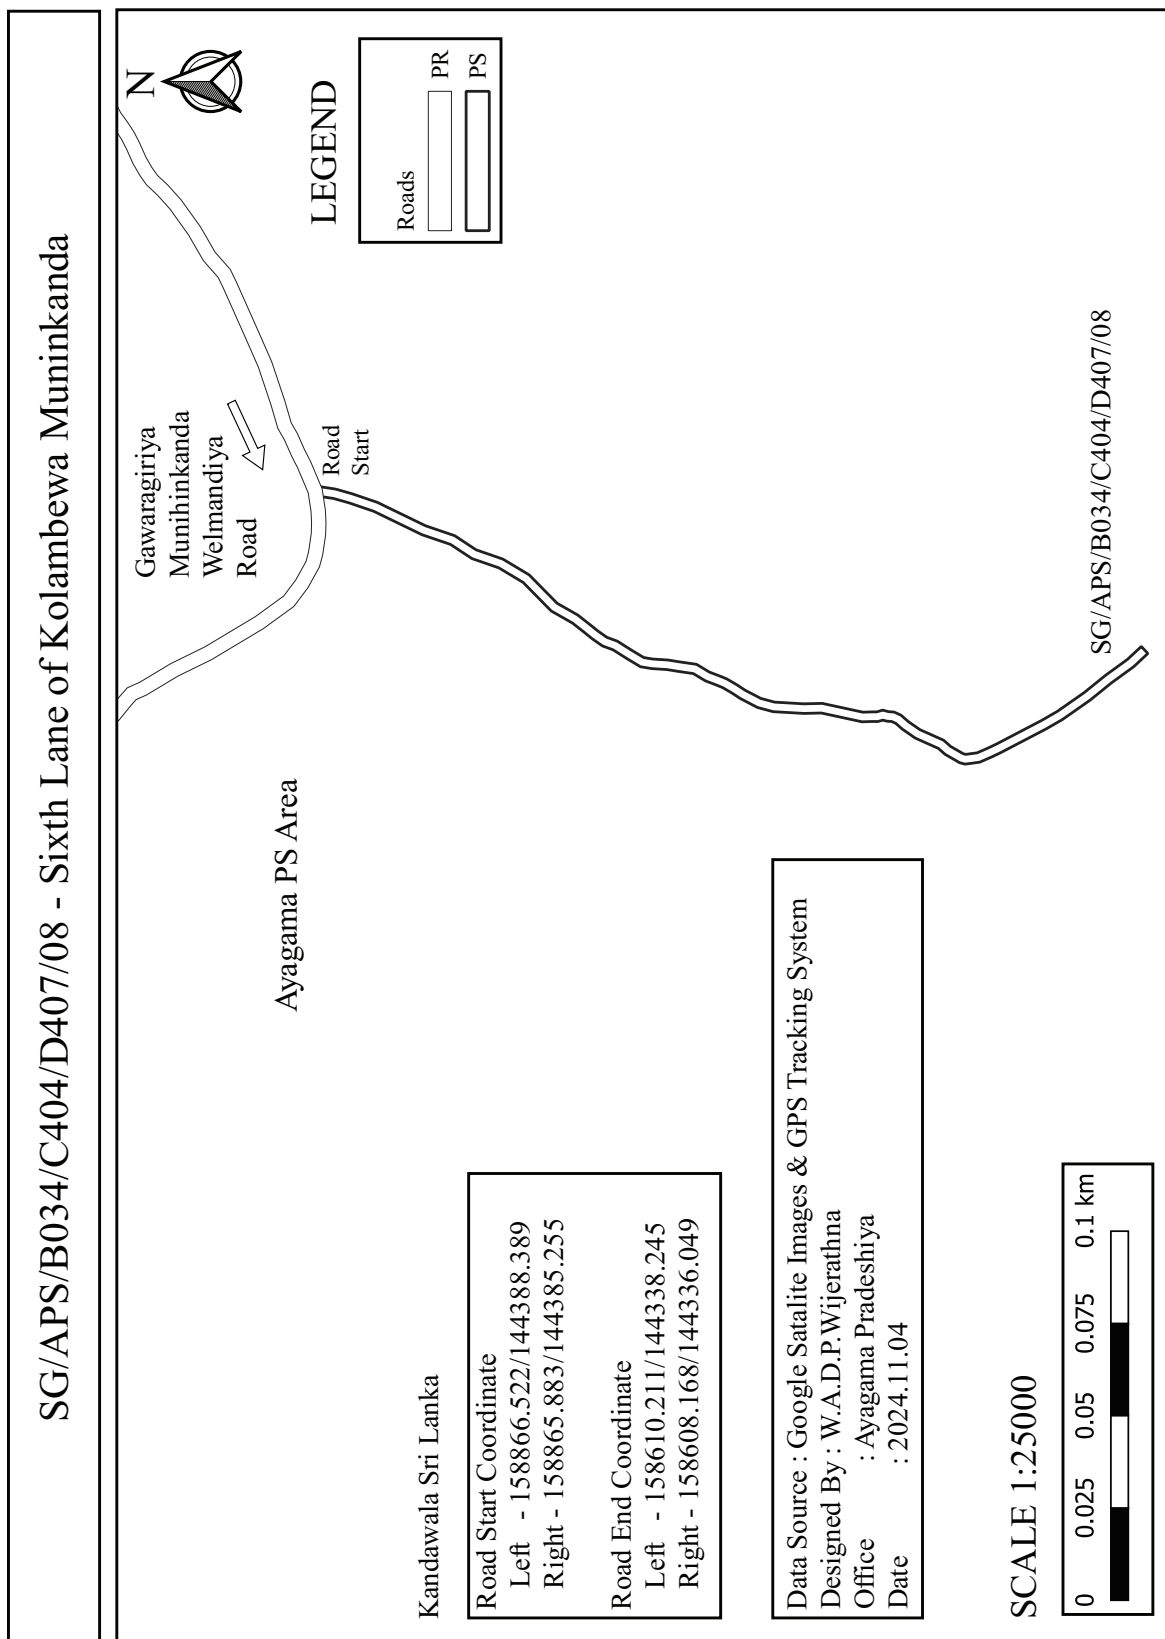


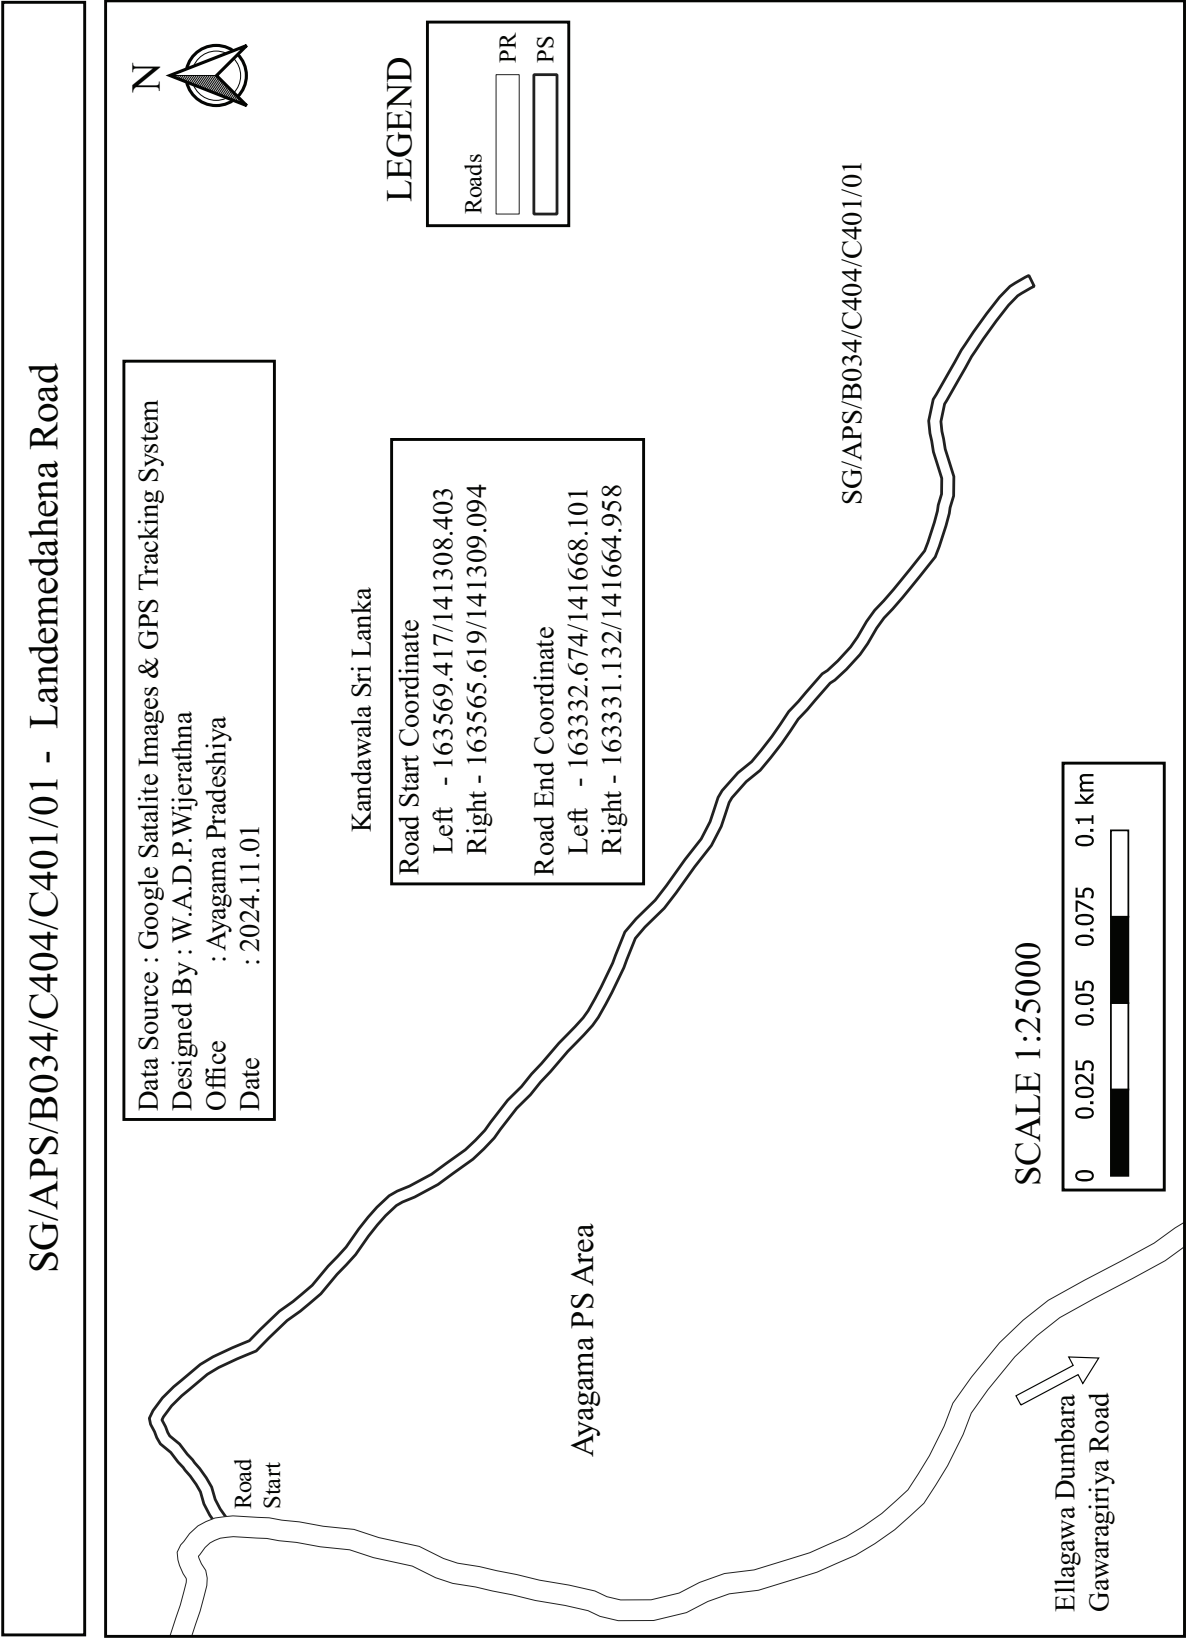


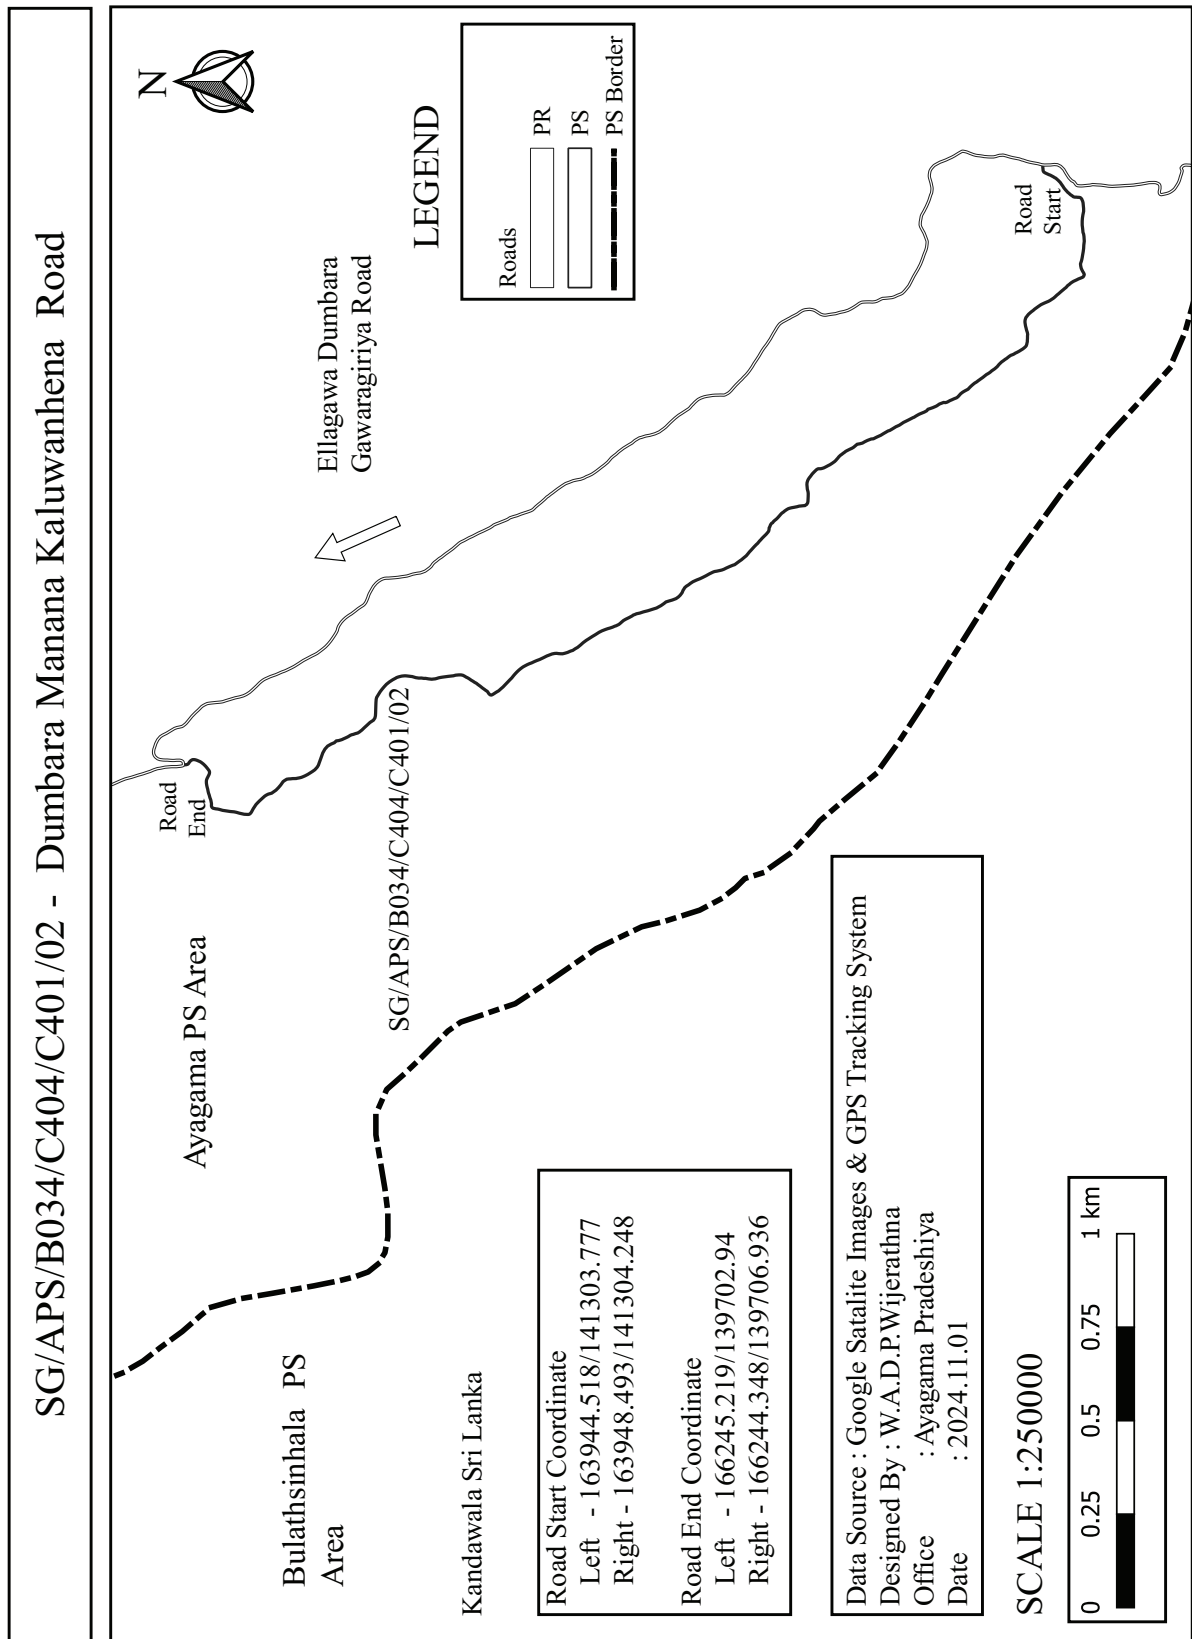


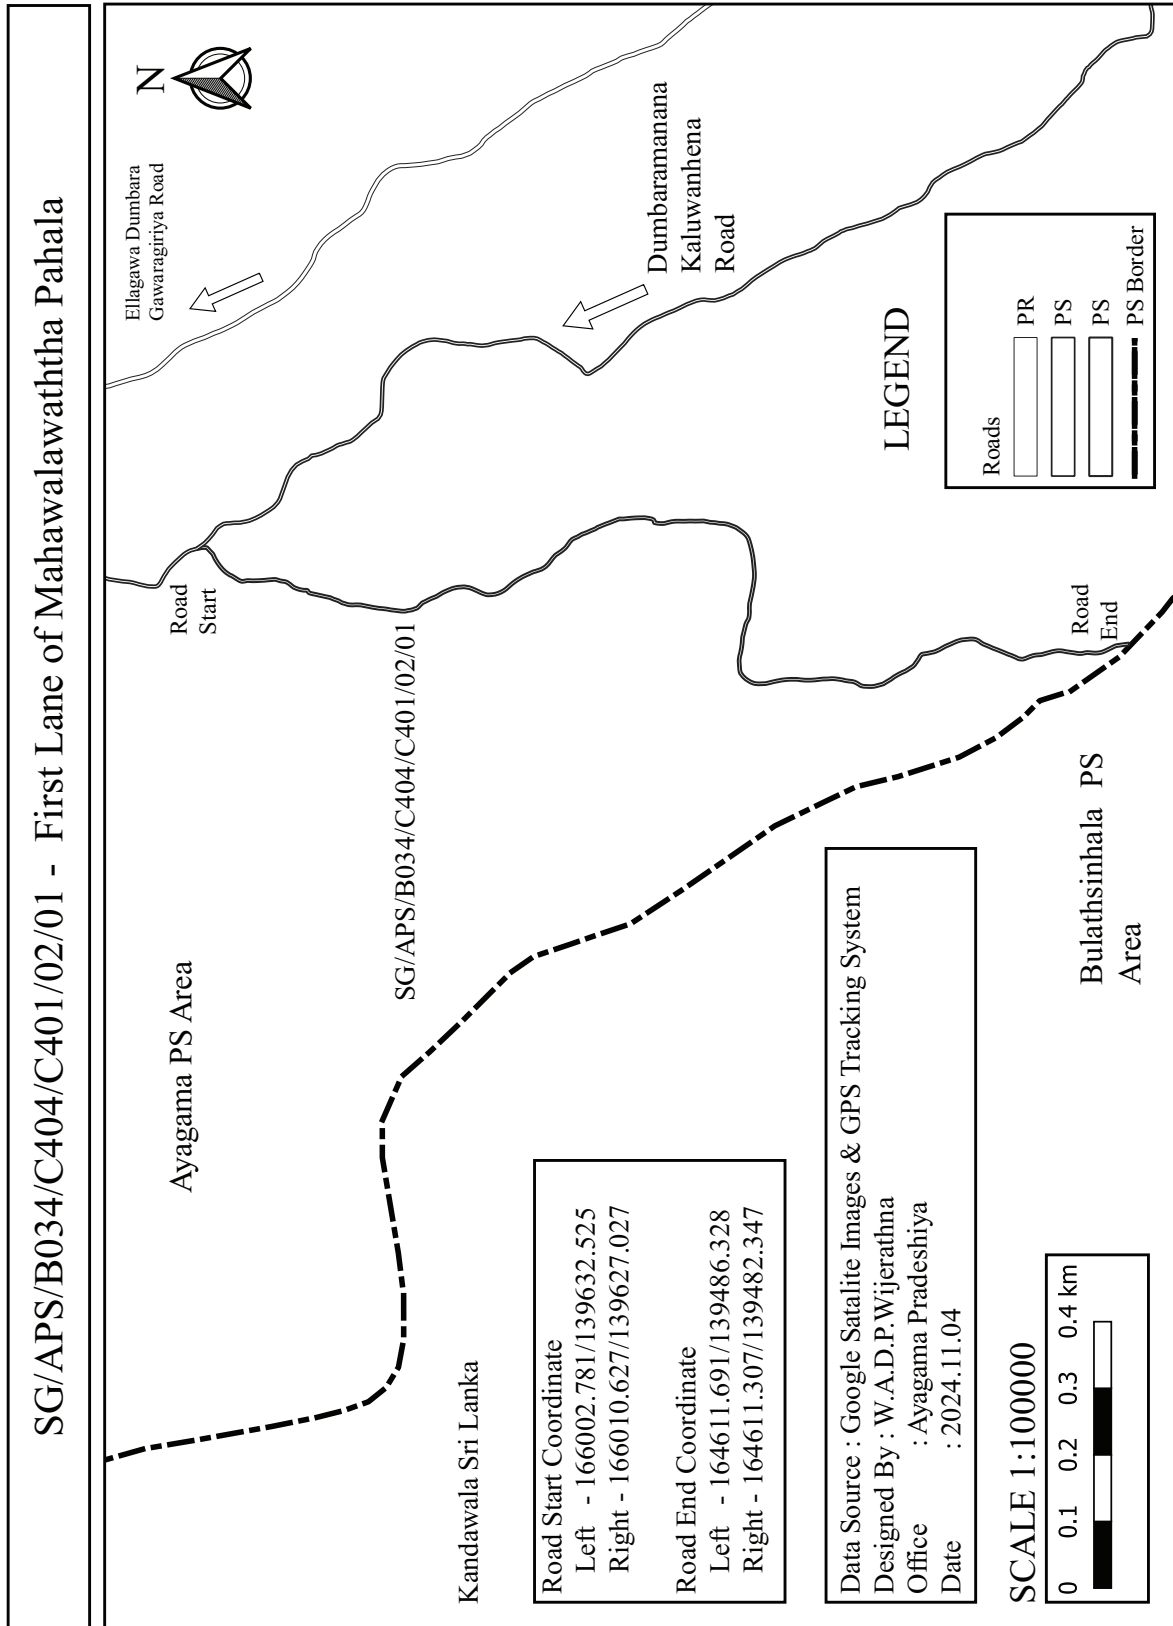


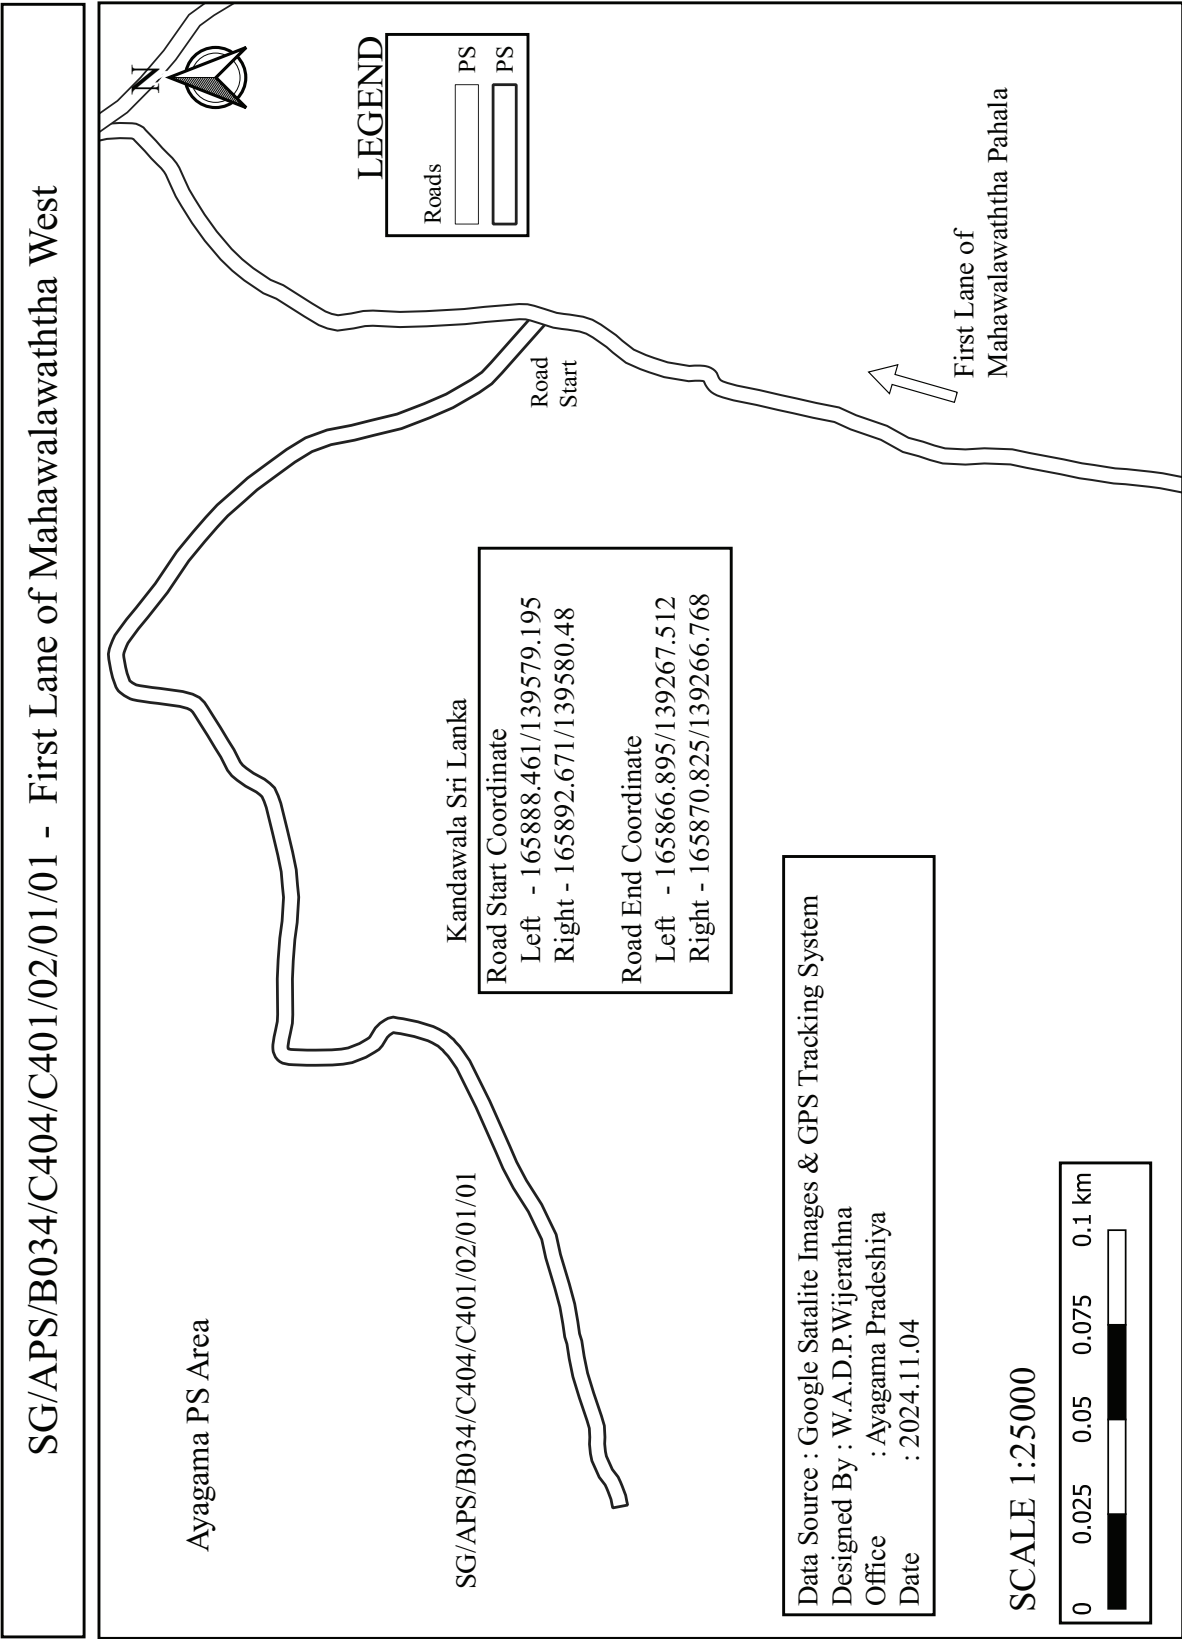


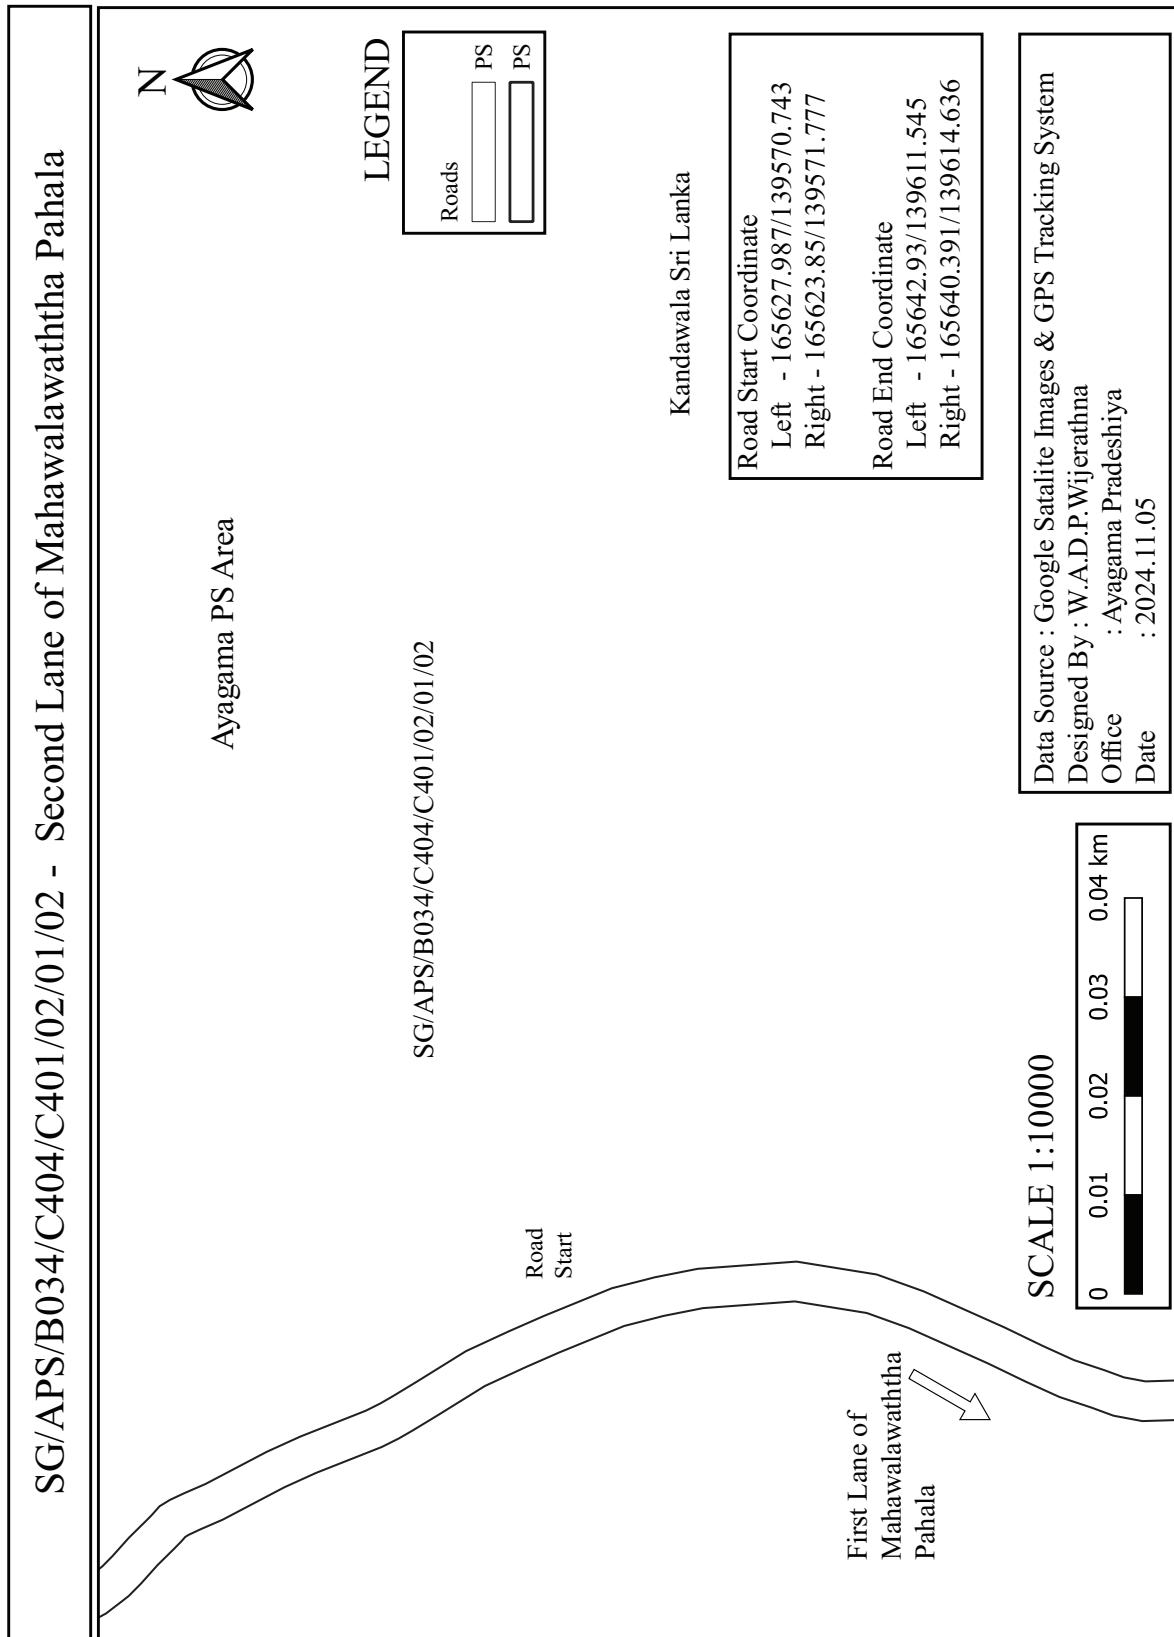


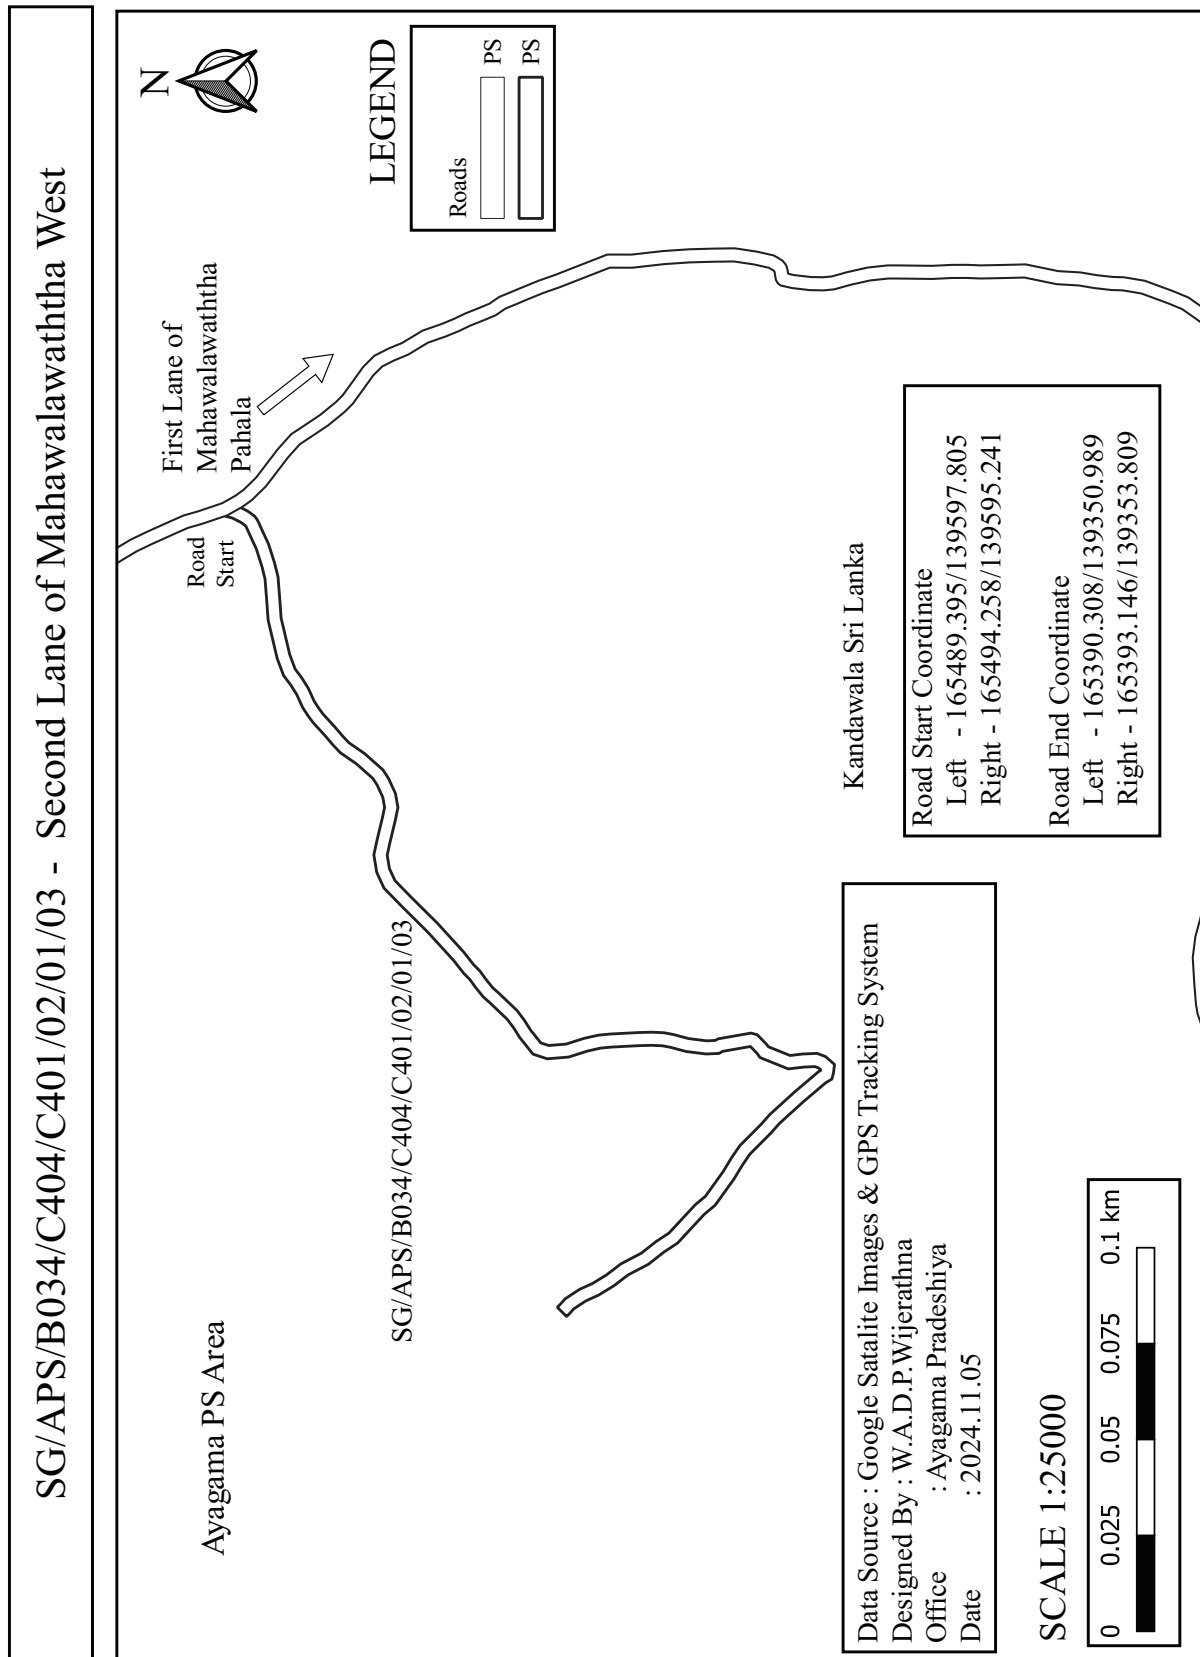


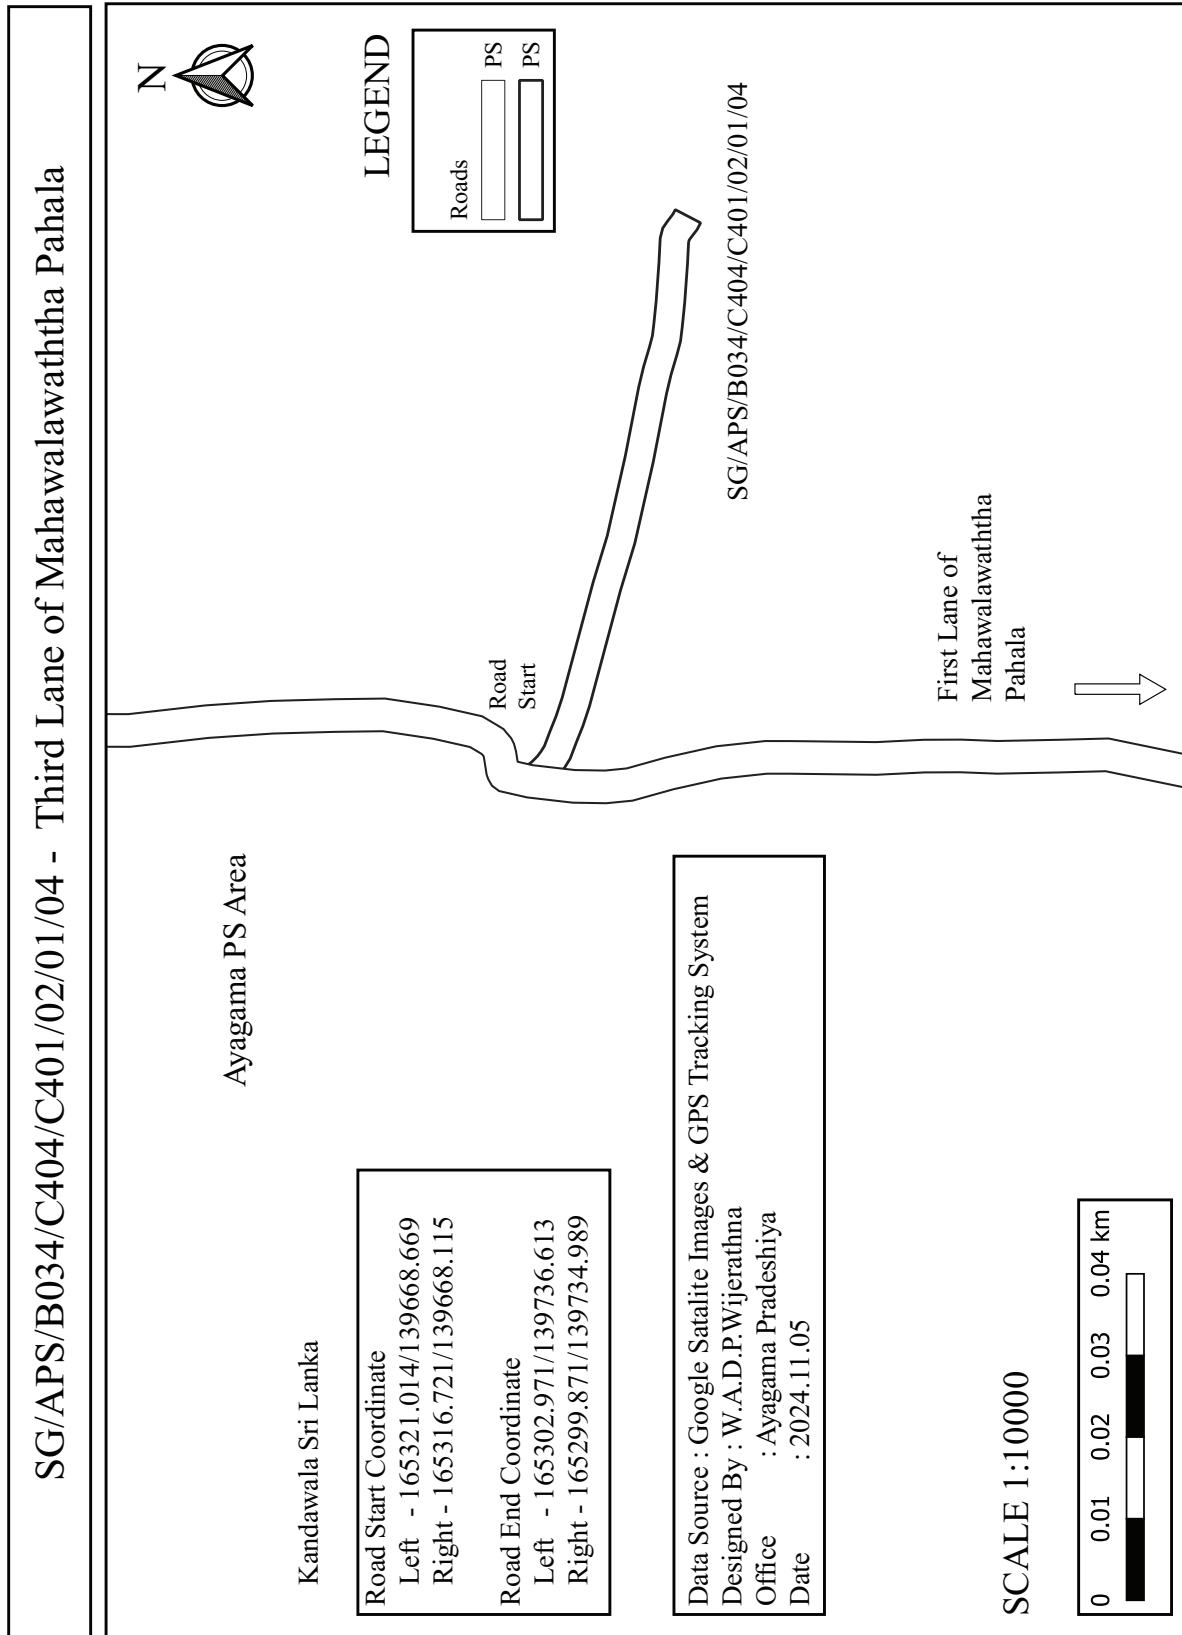


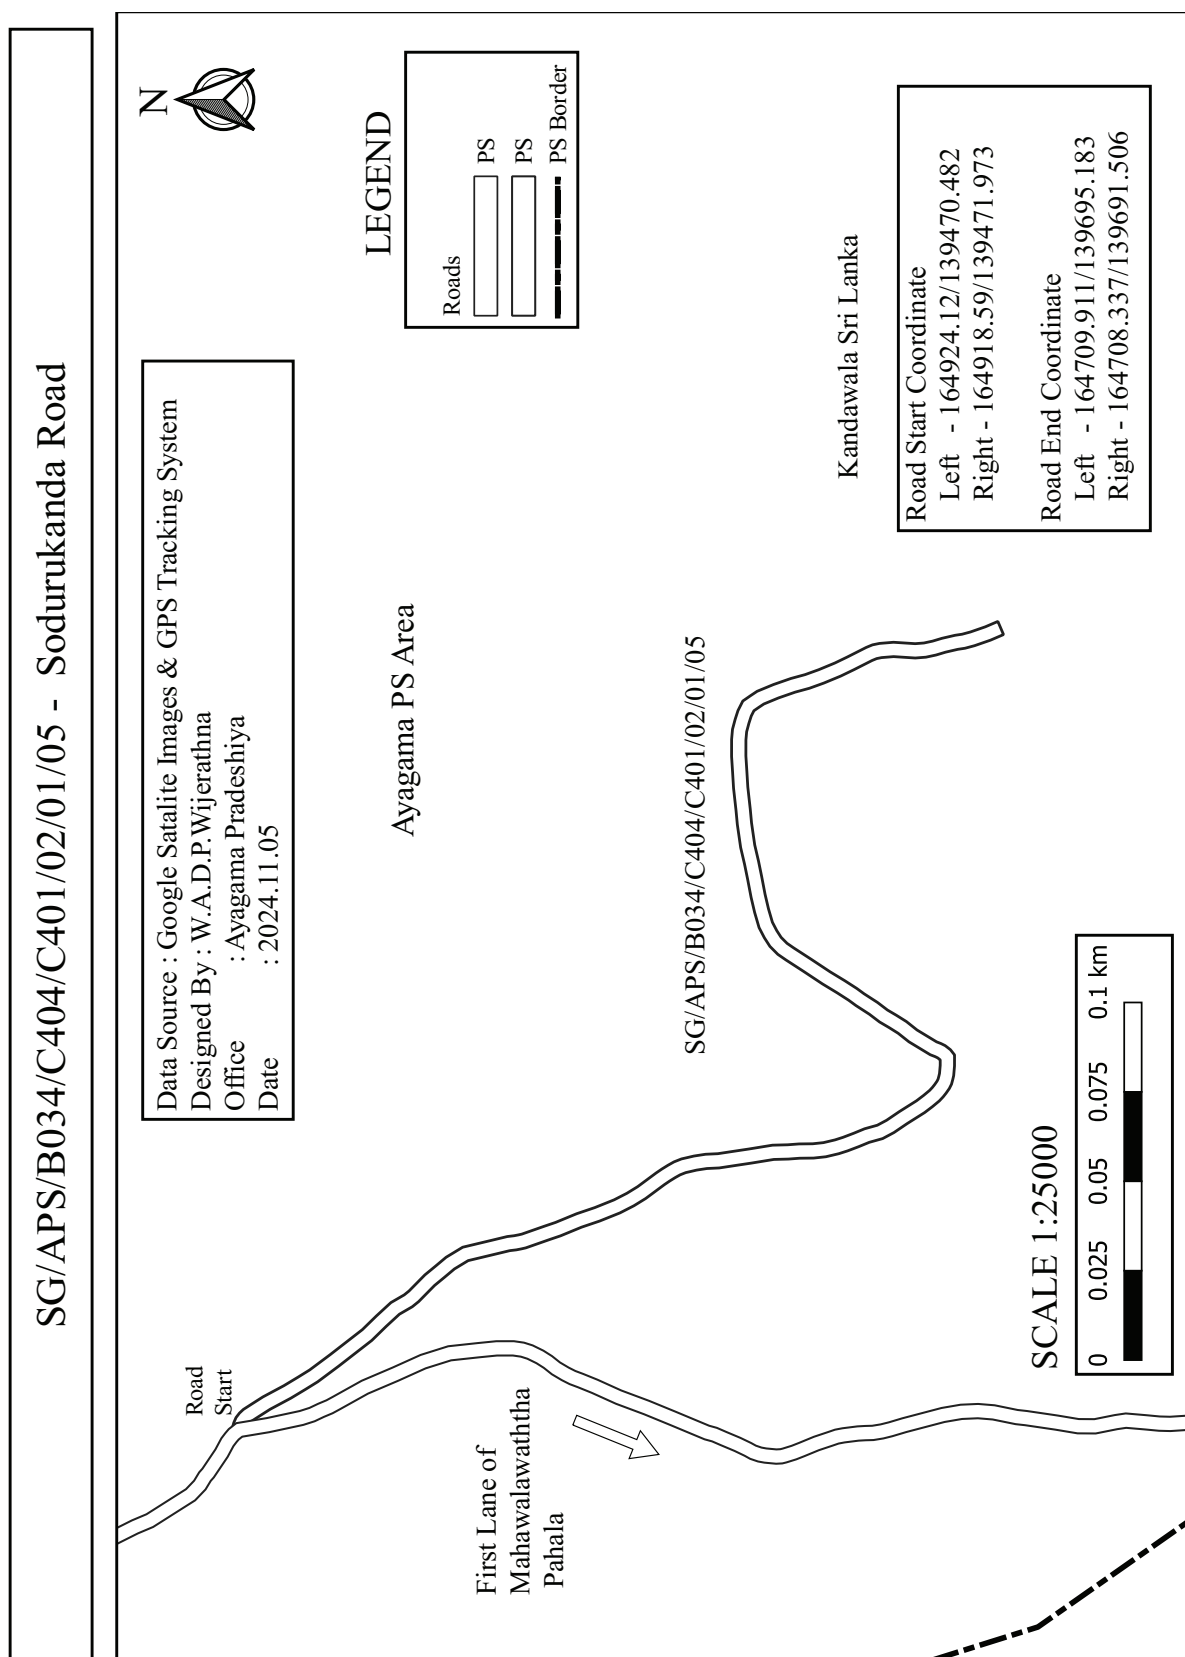

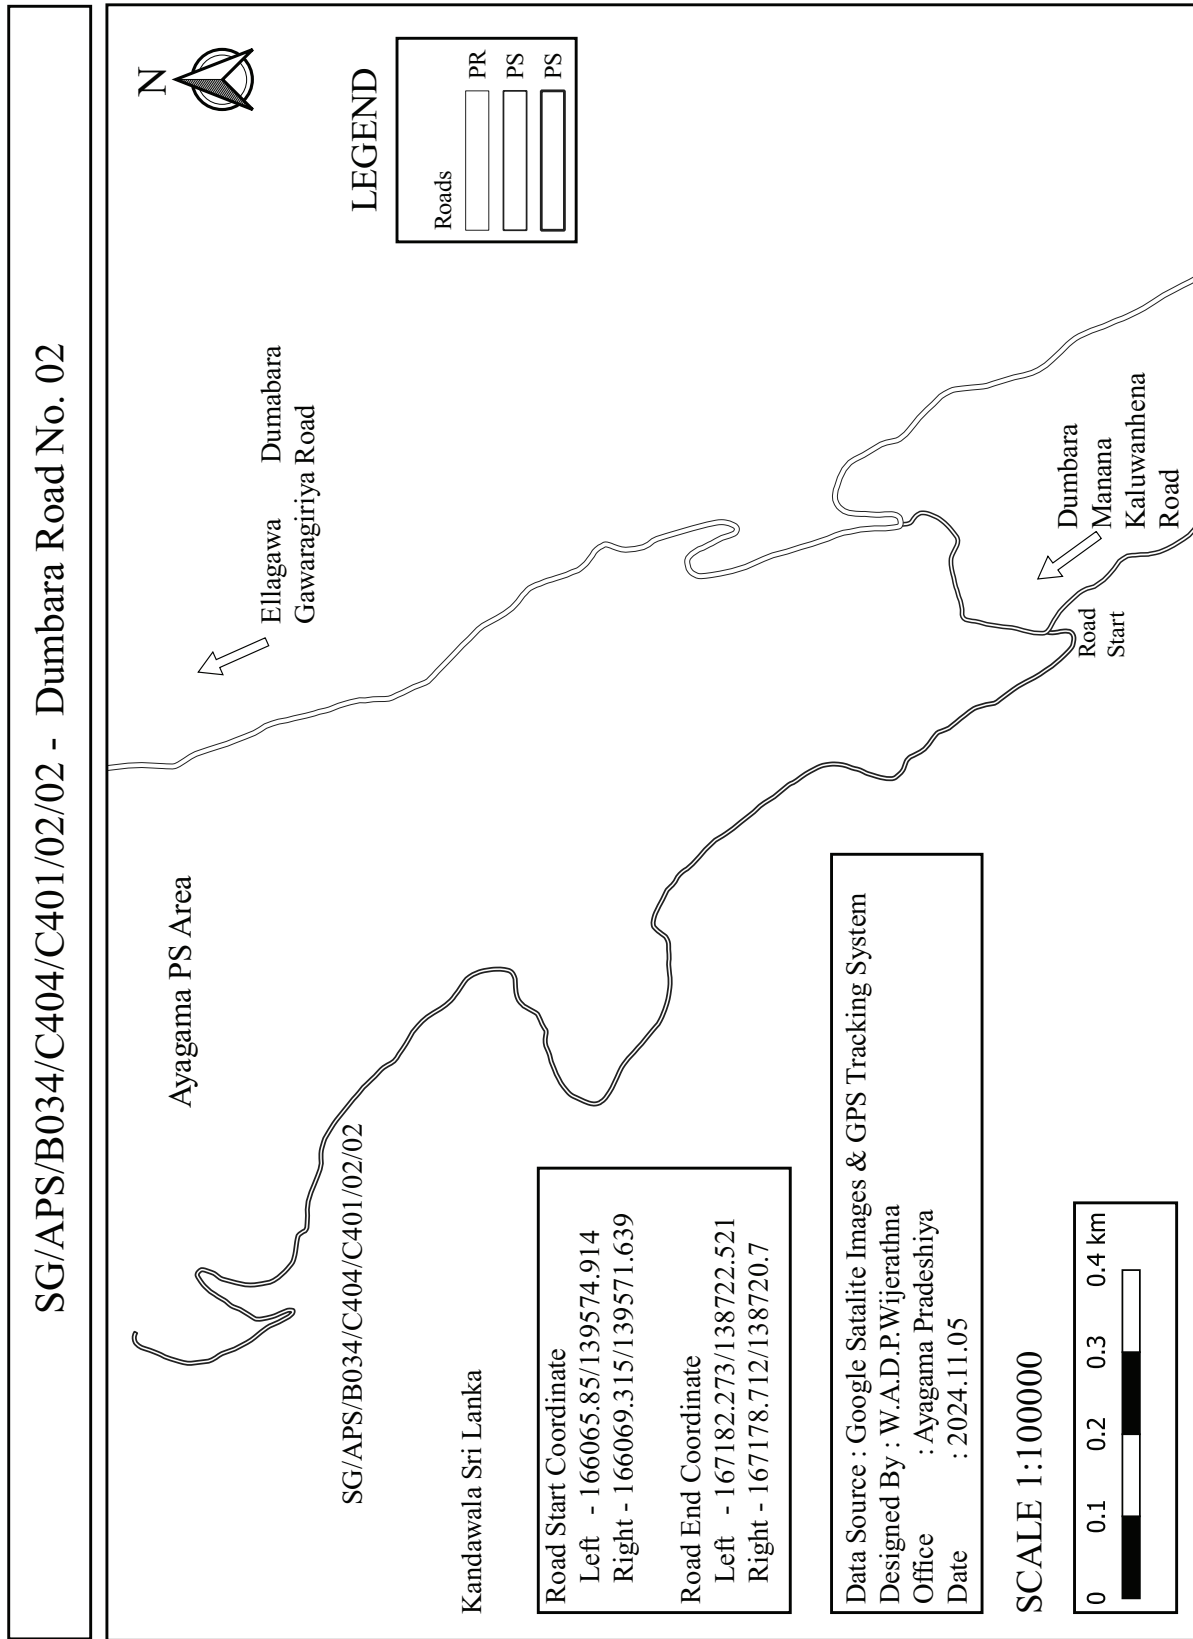


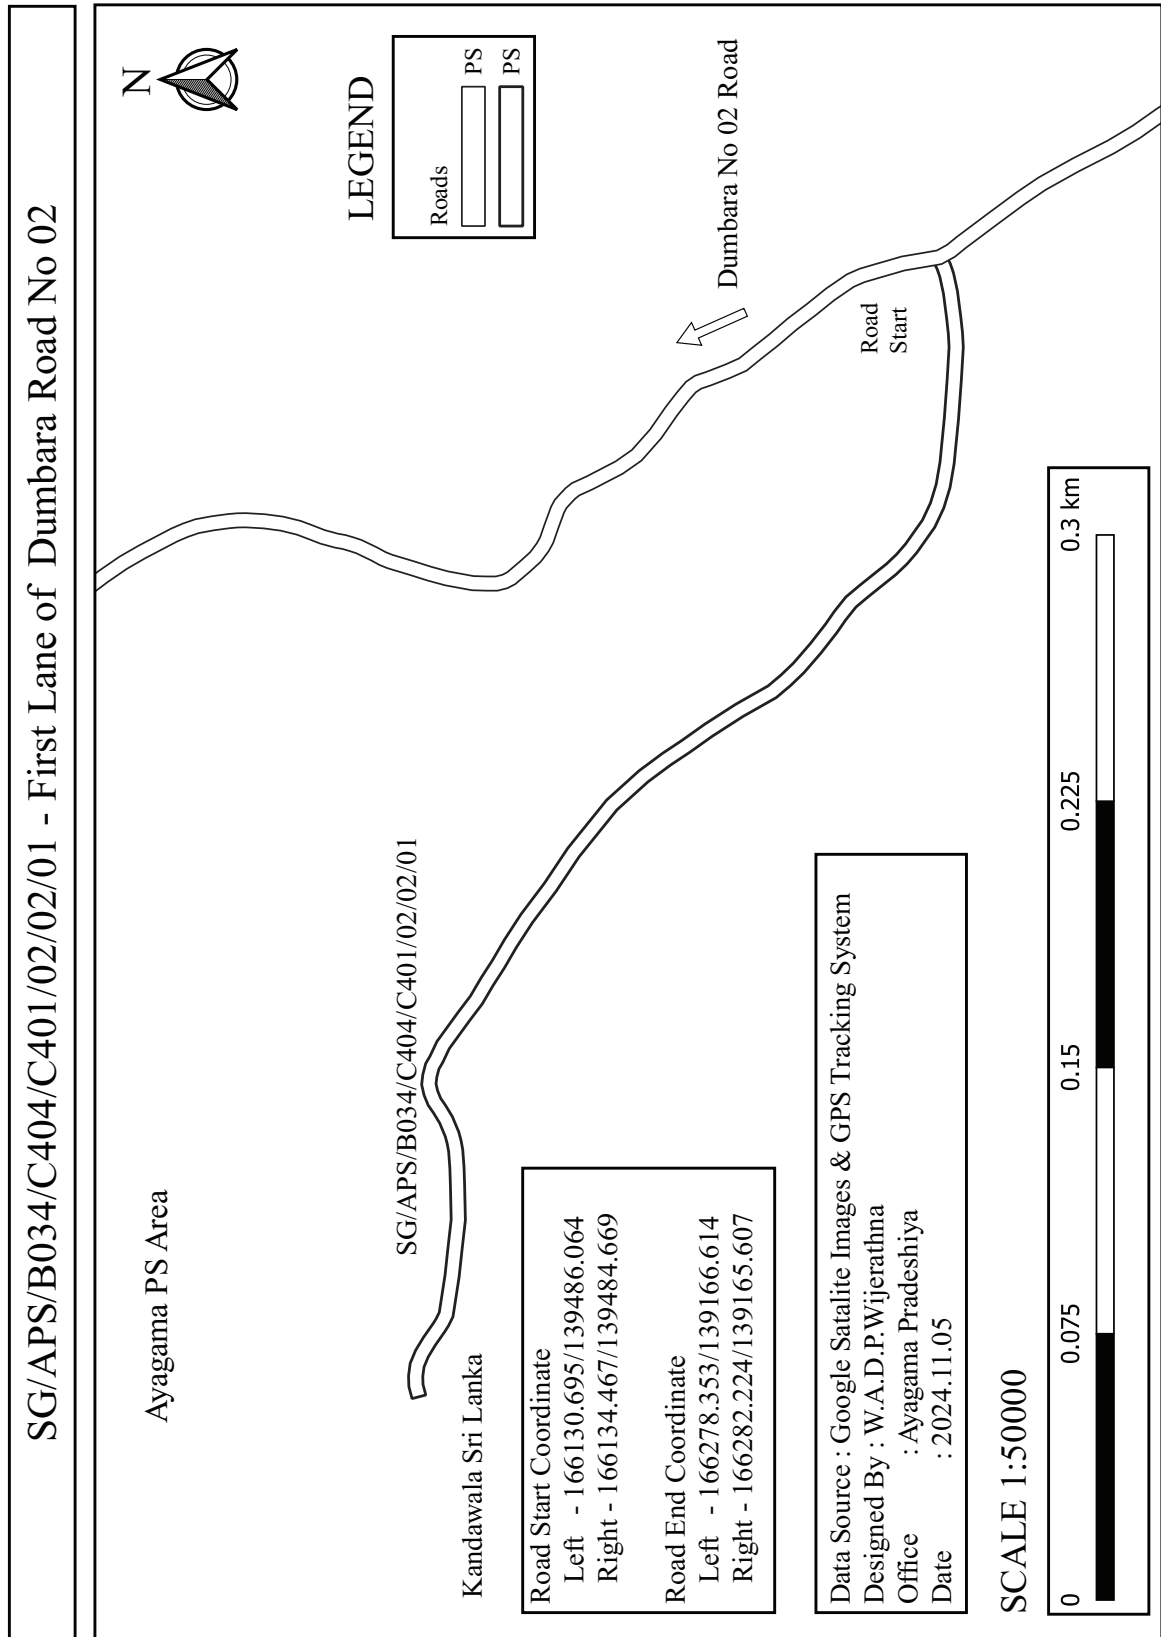


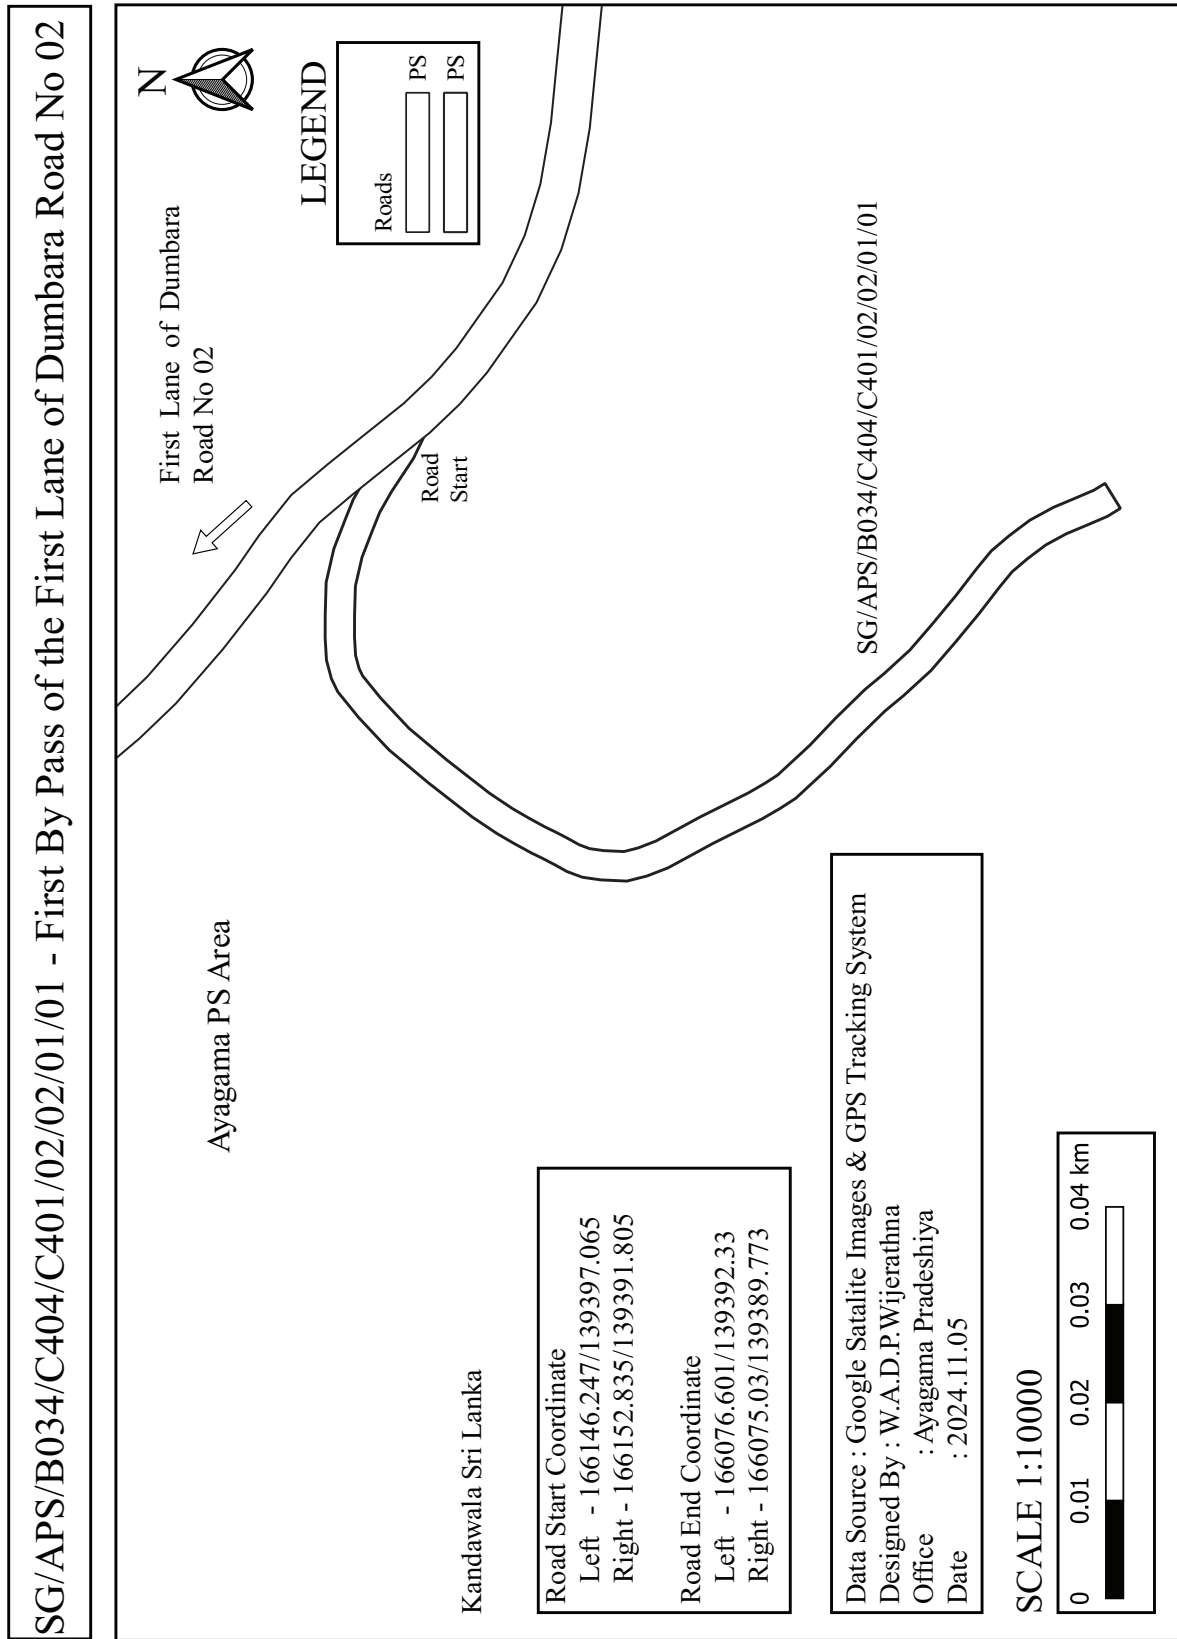


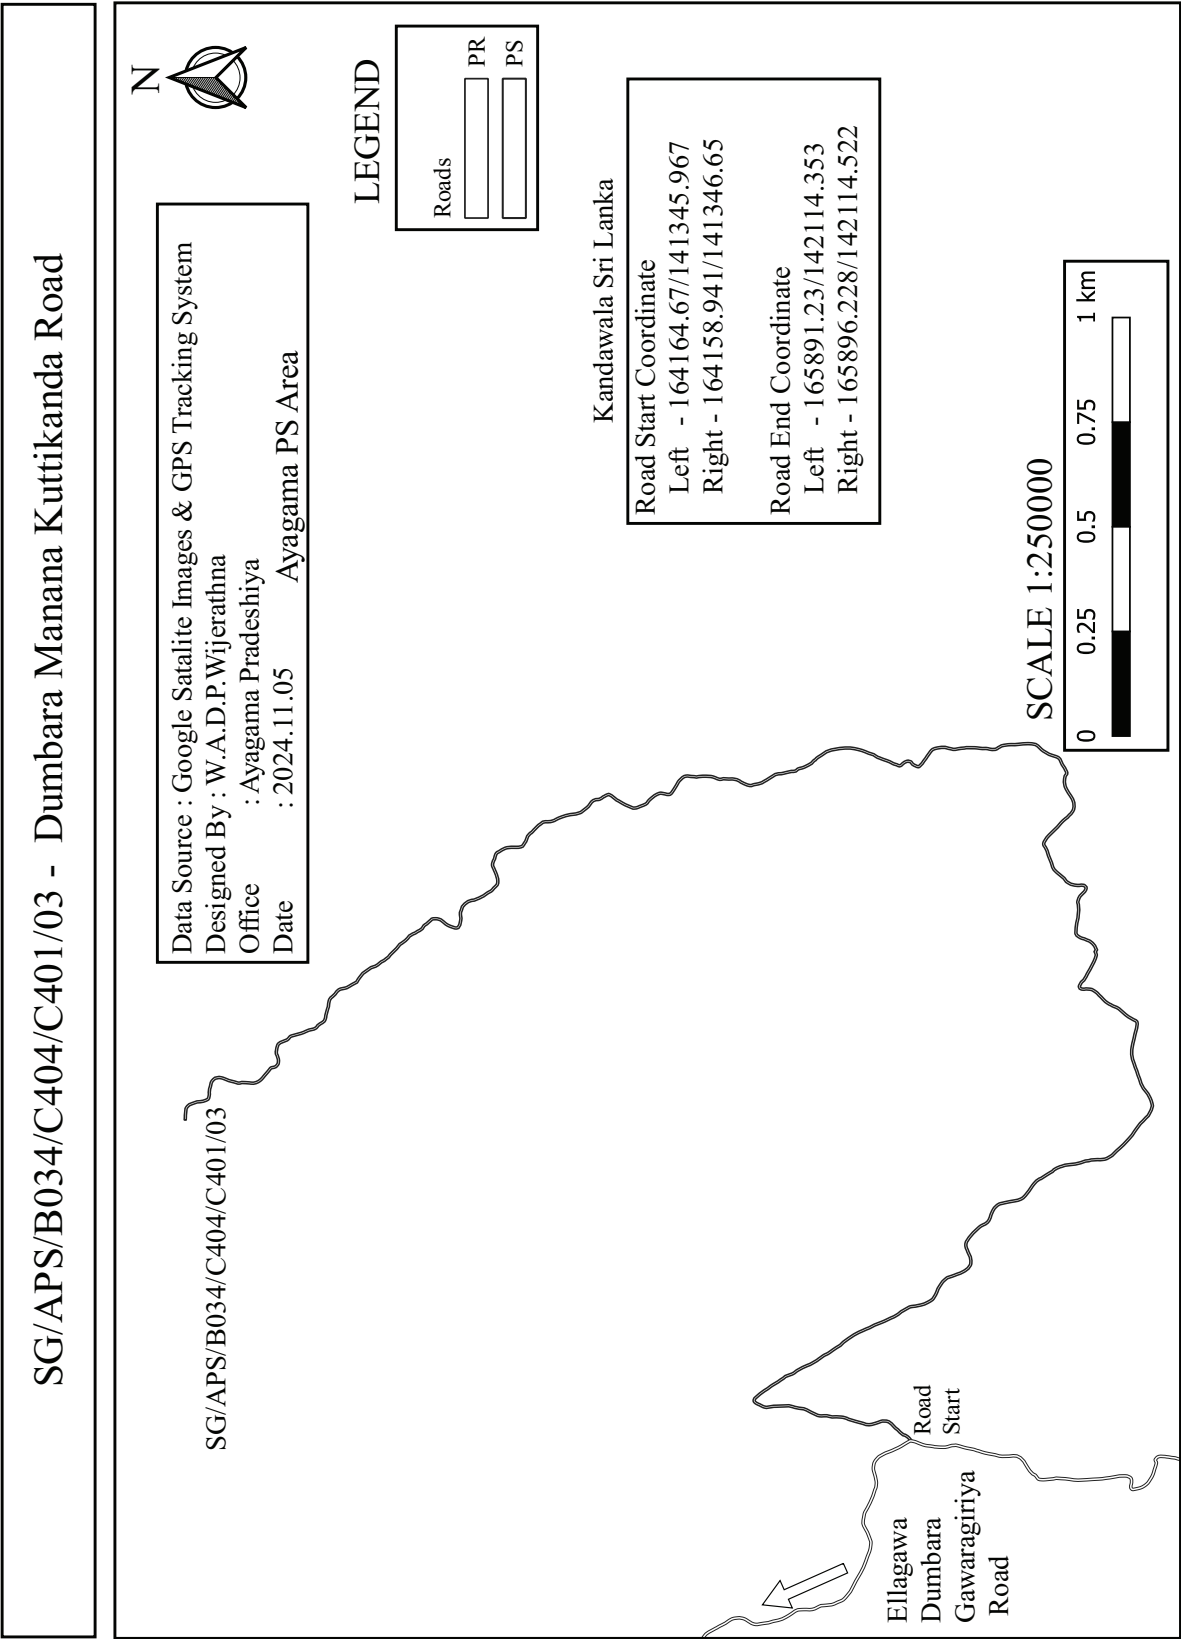



SG/APS/B034/C404/C401/03/01 - No. 01 Dumbara Manana Road

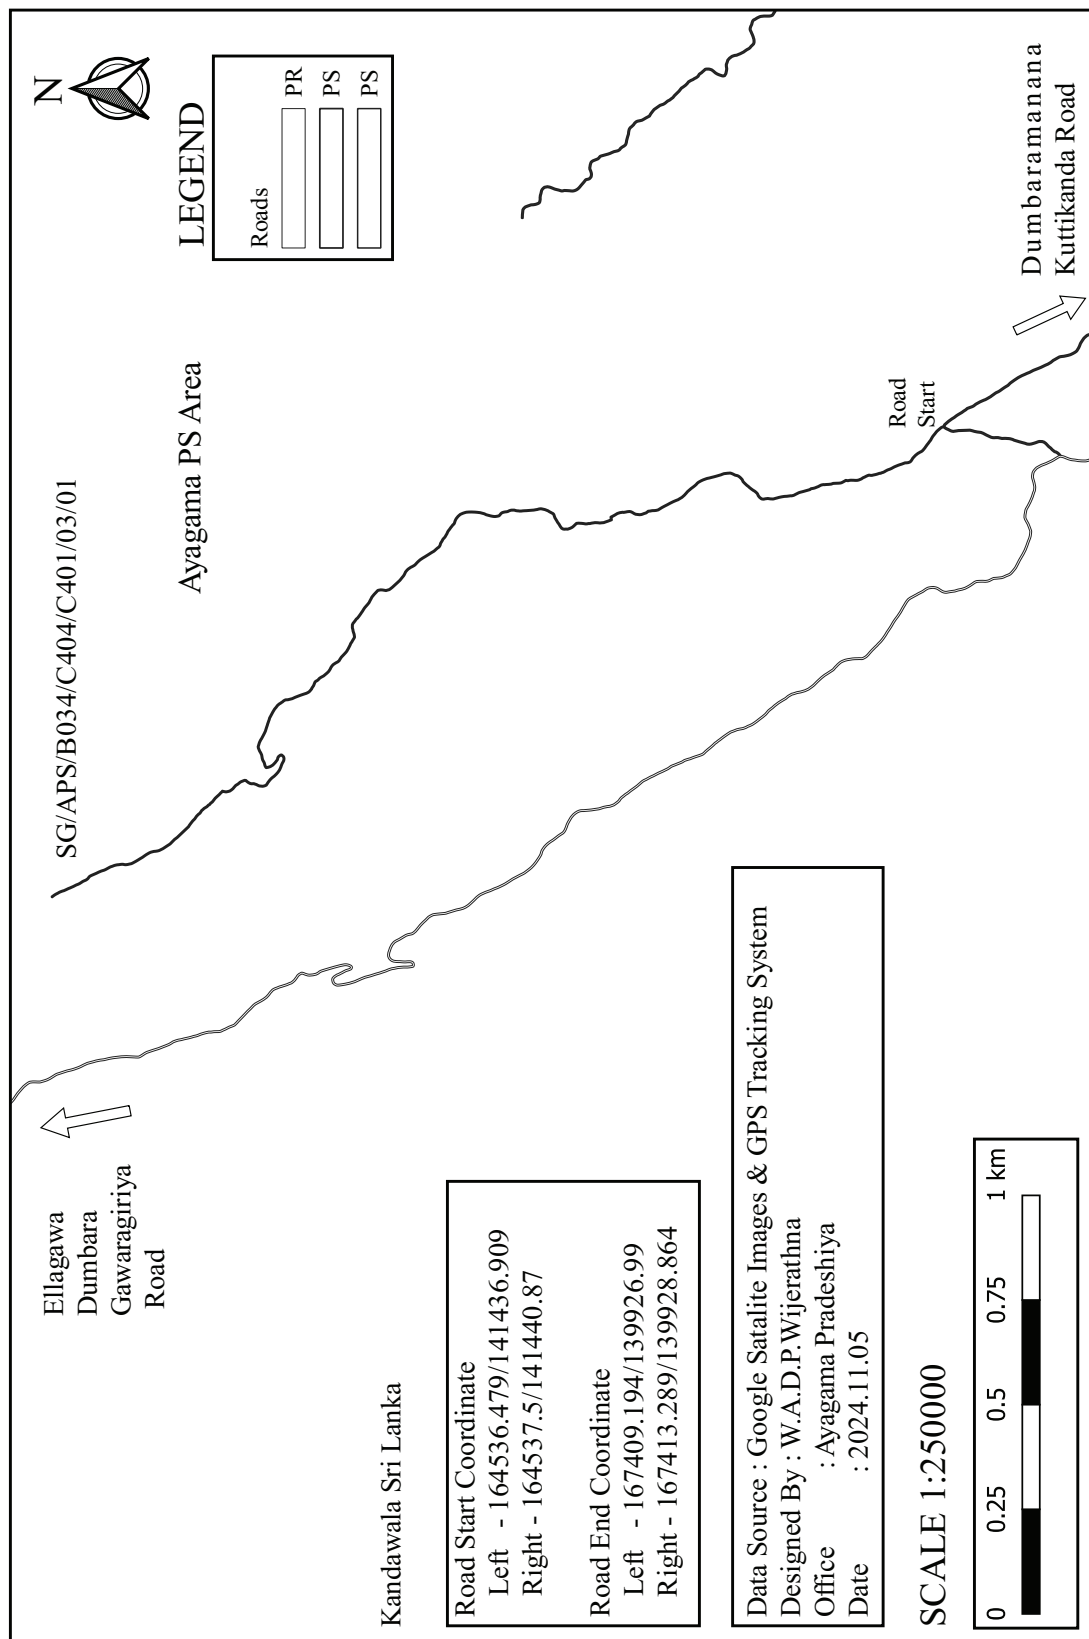


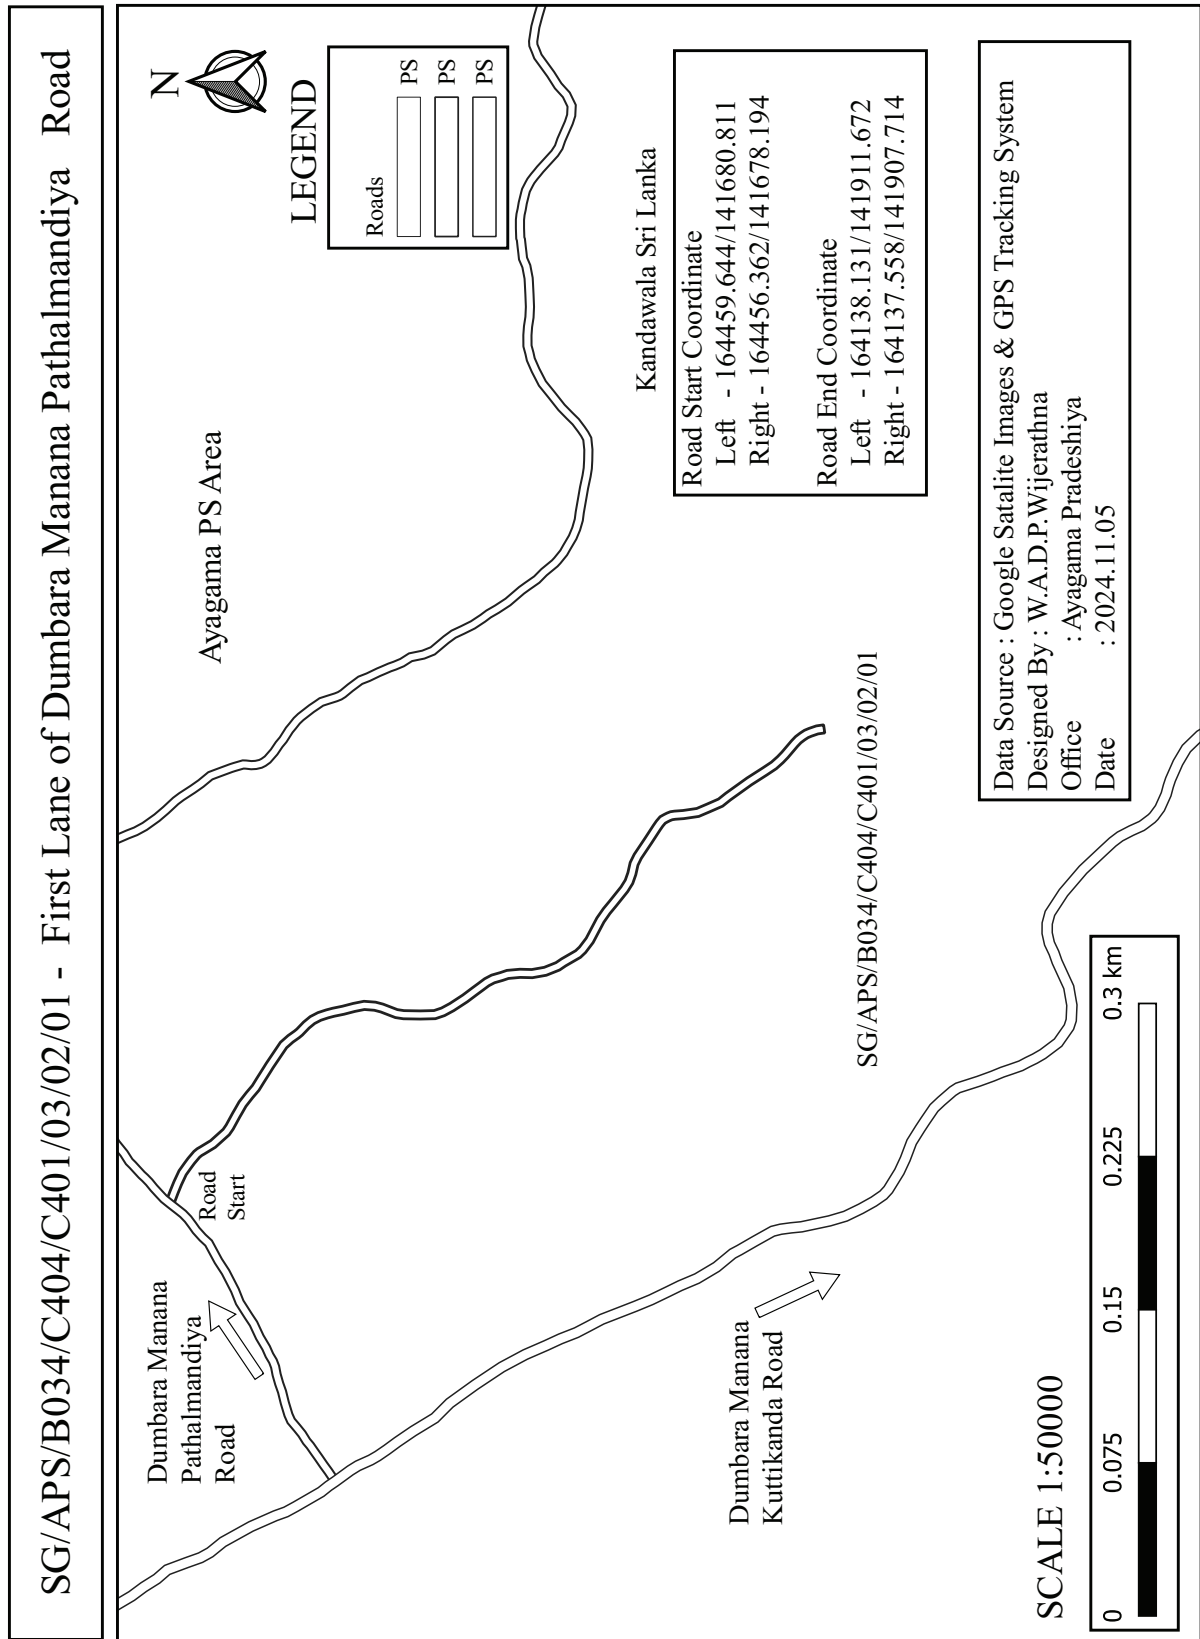


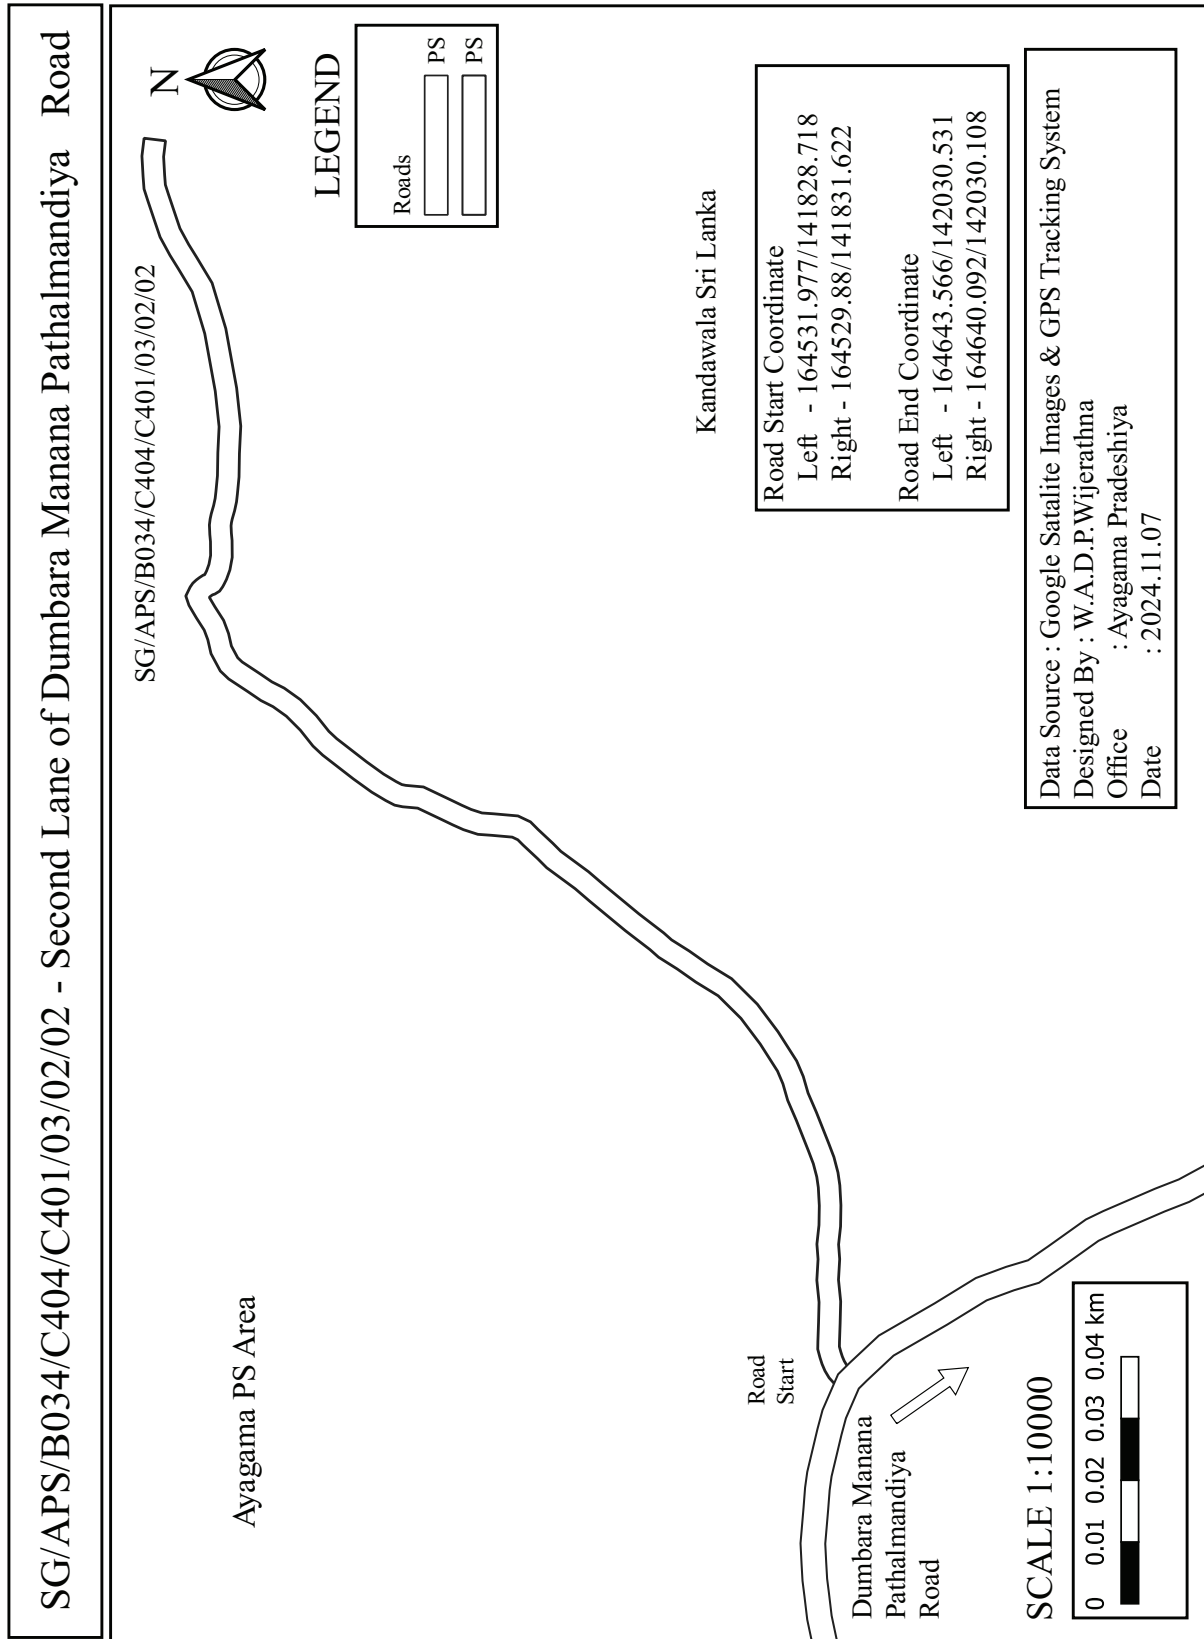


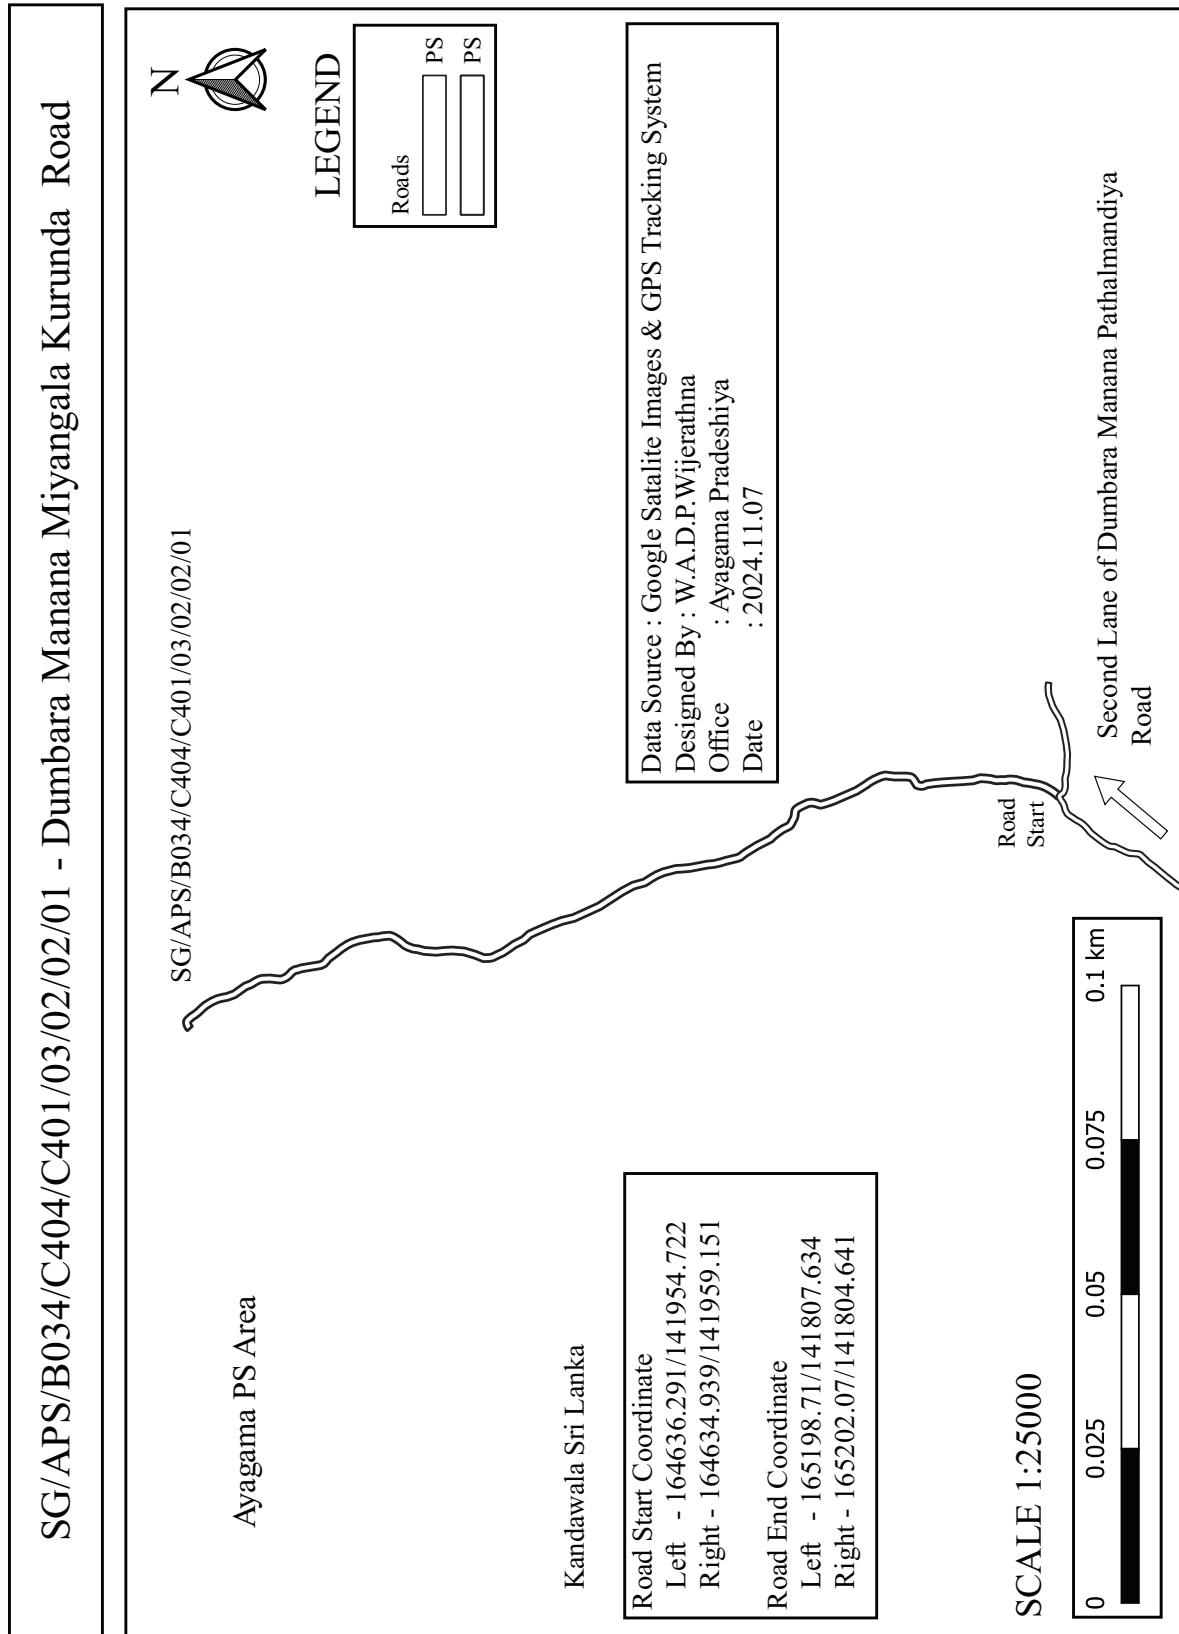


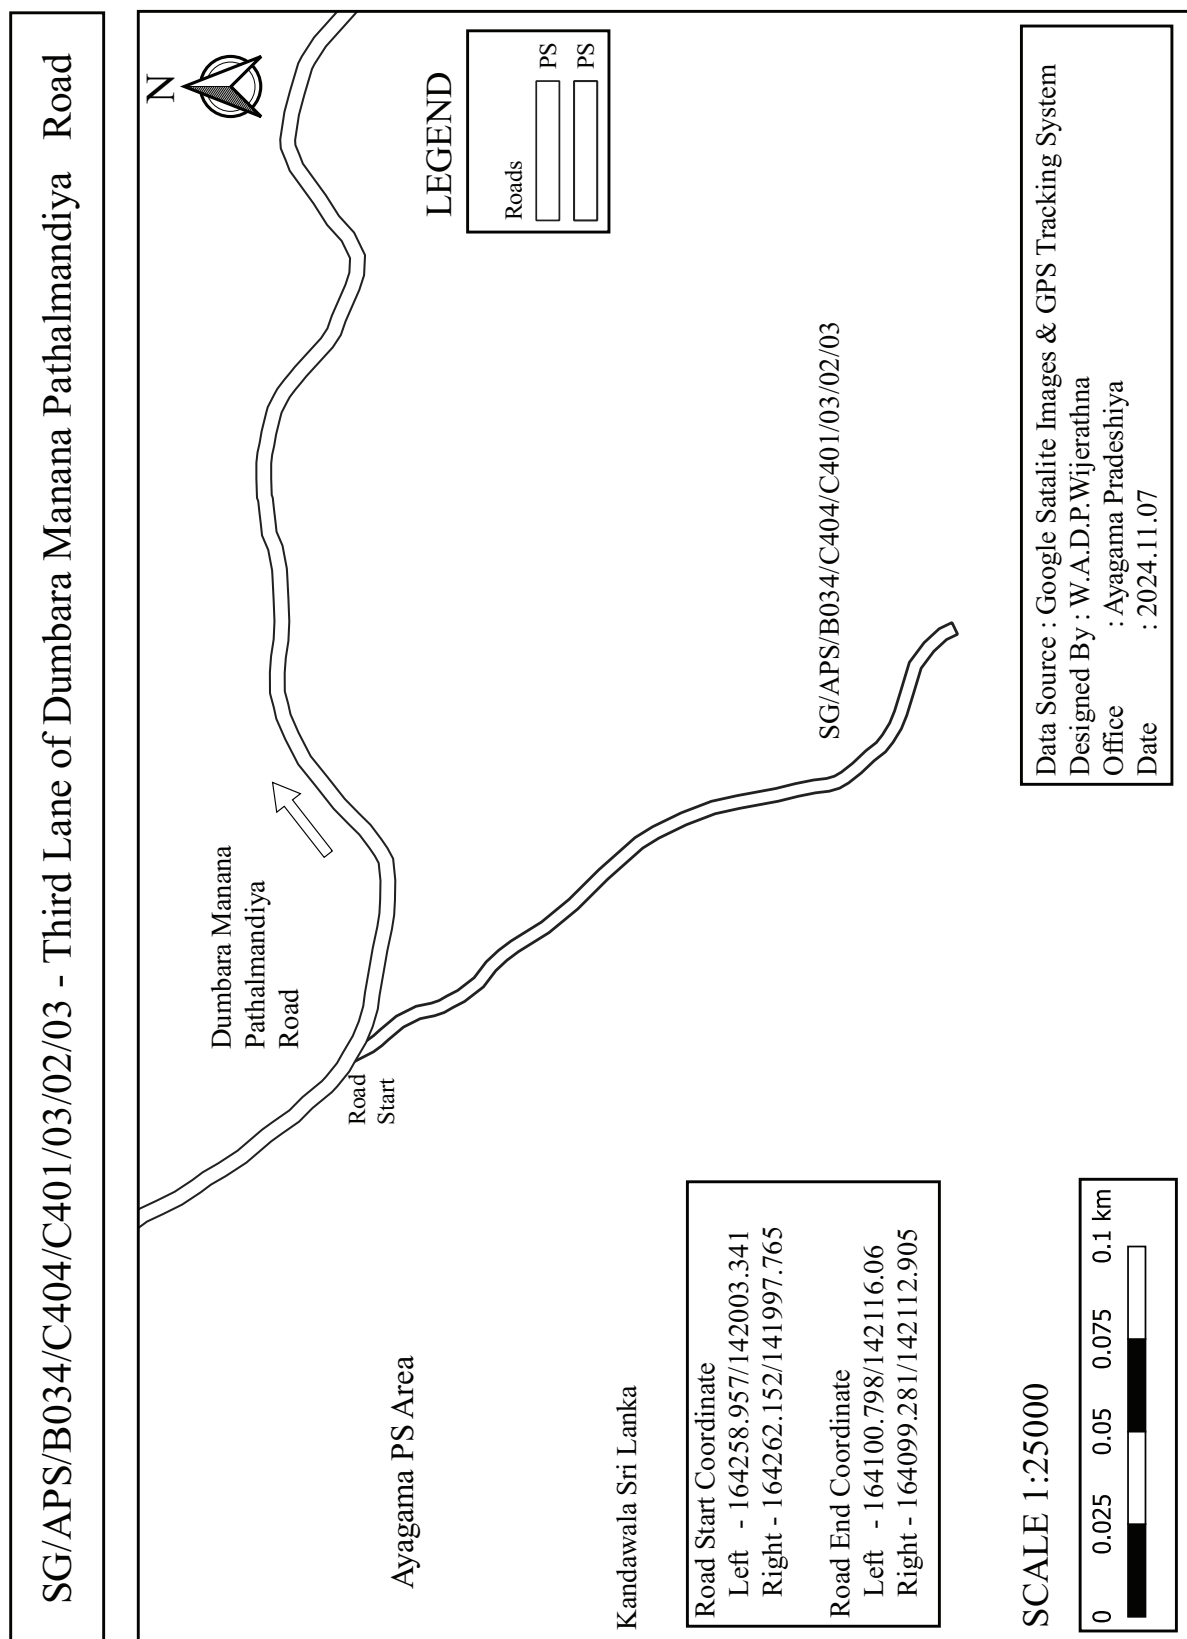


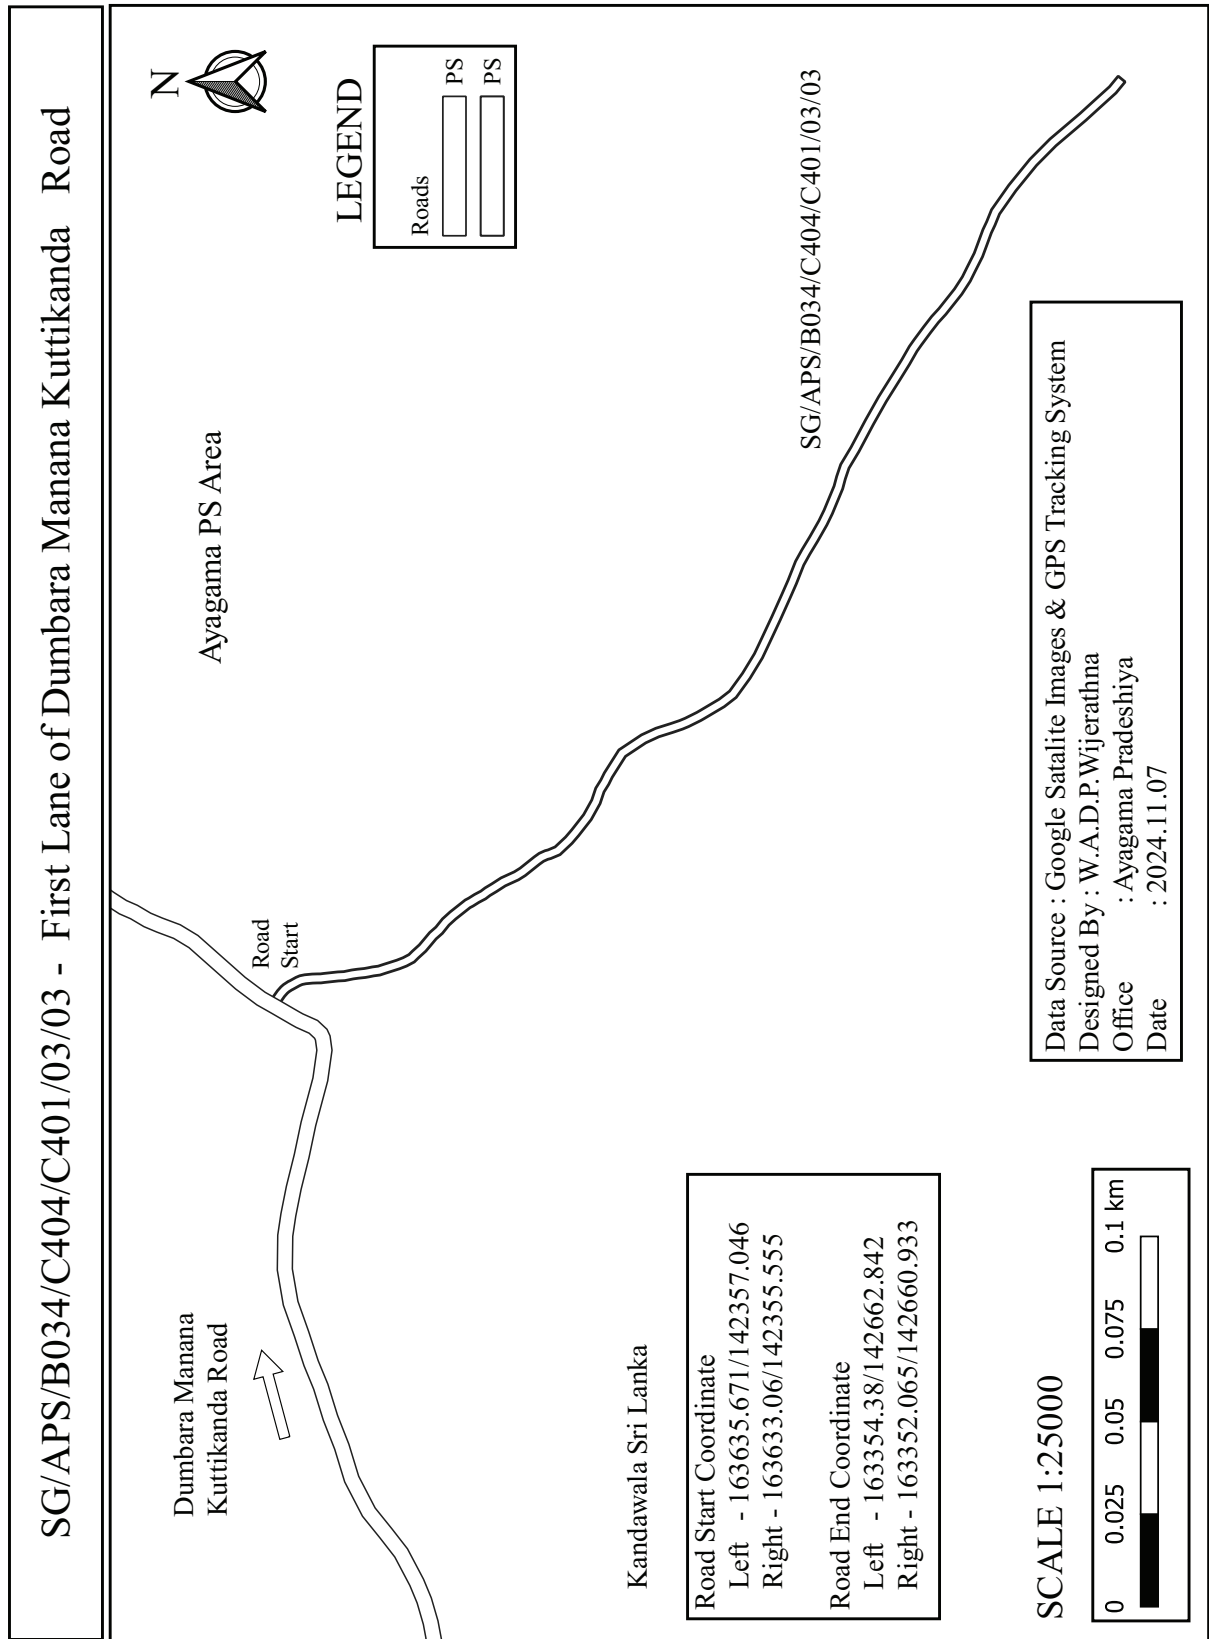


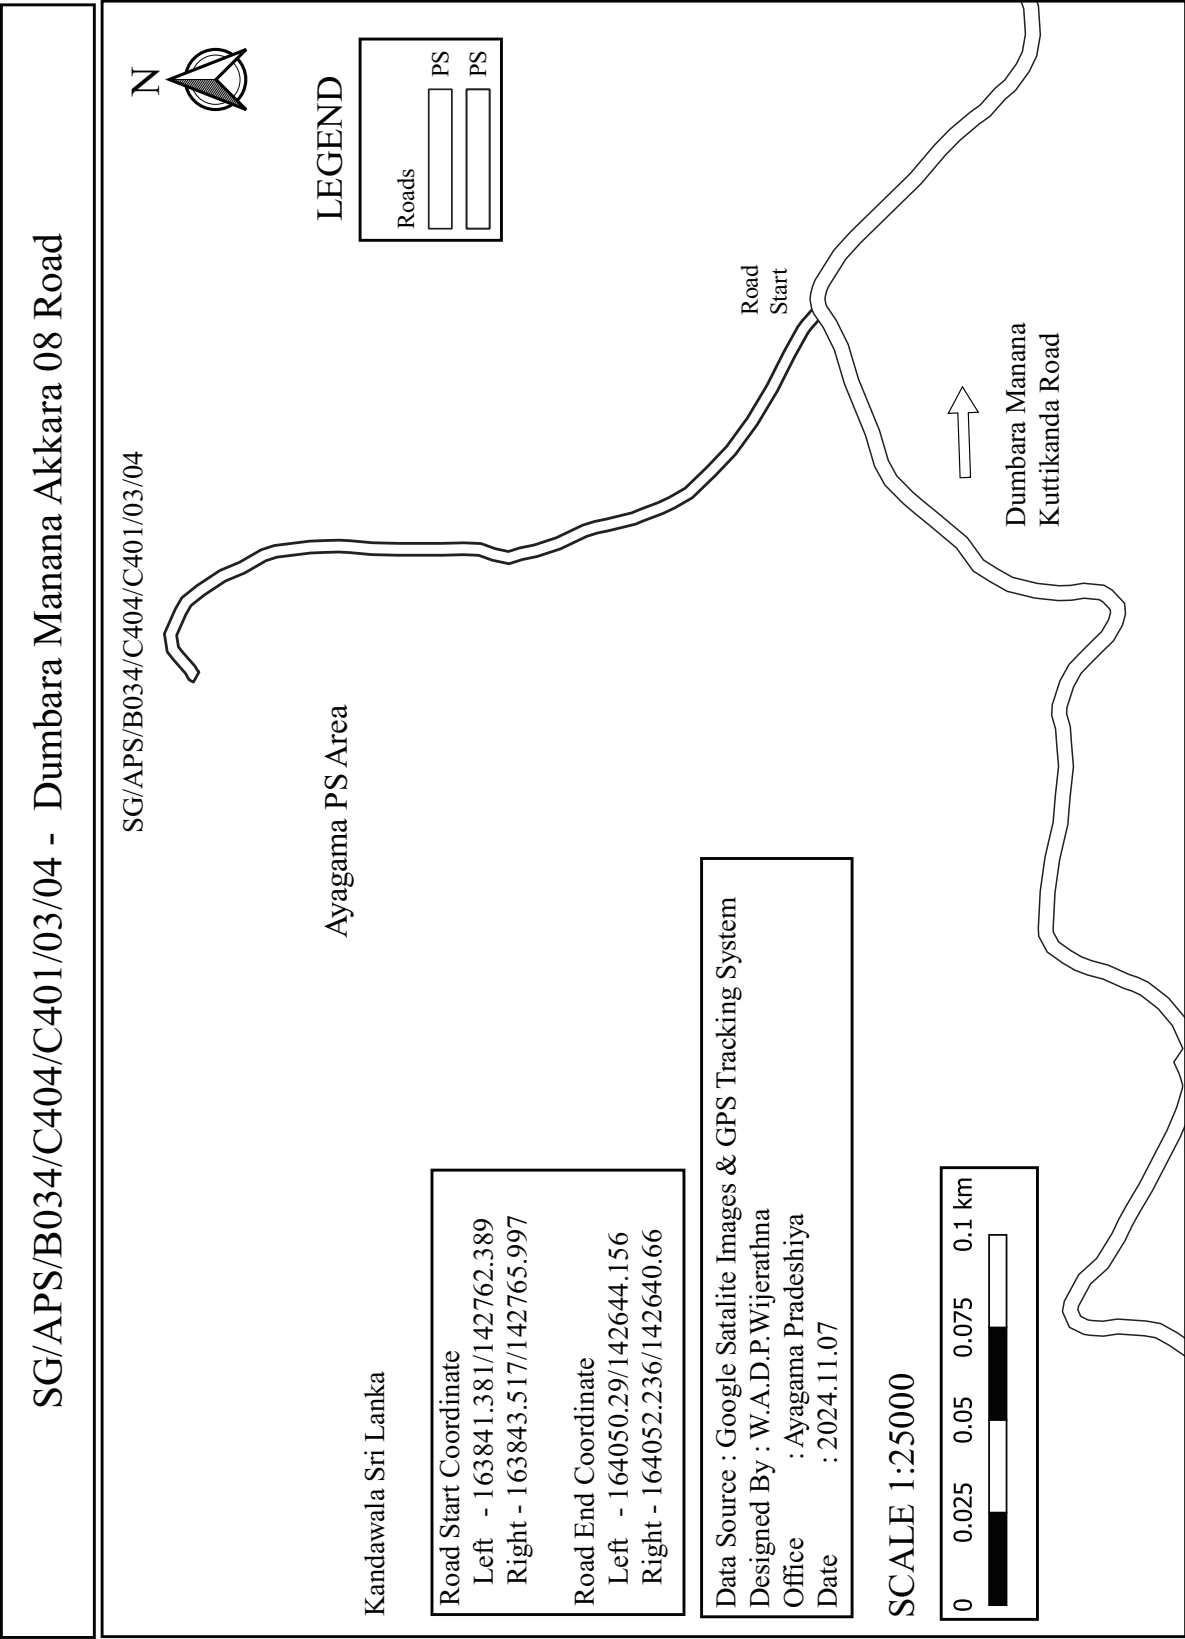


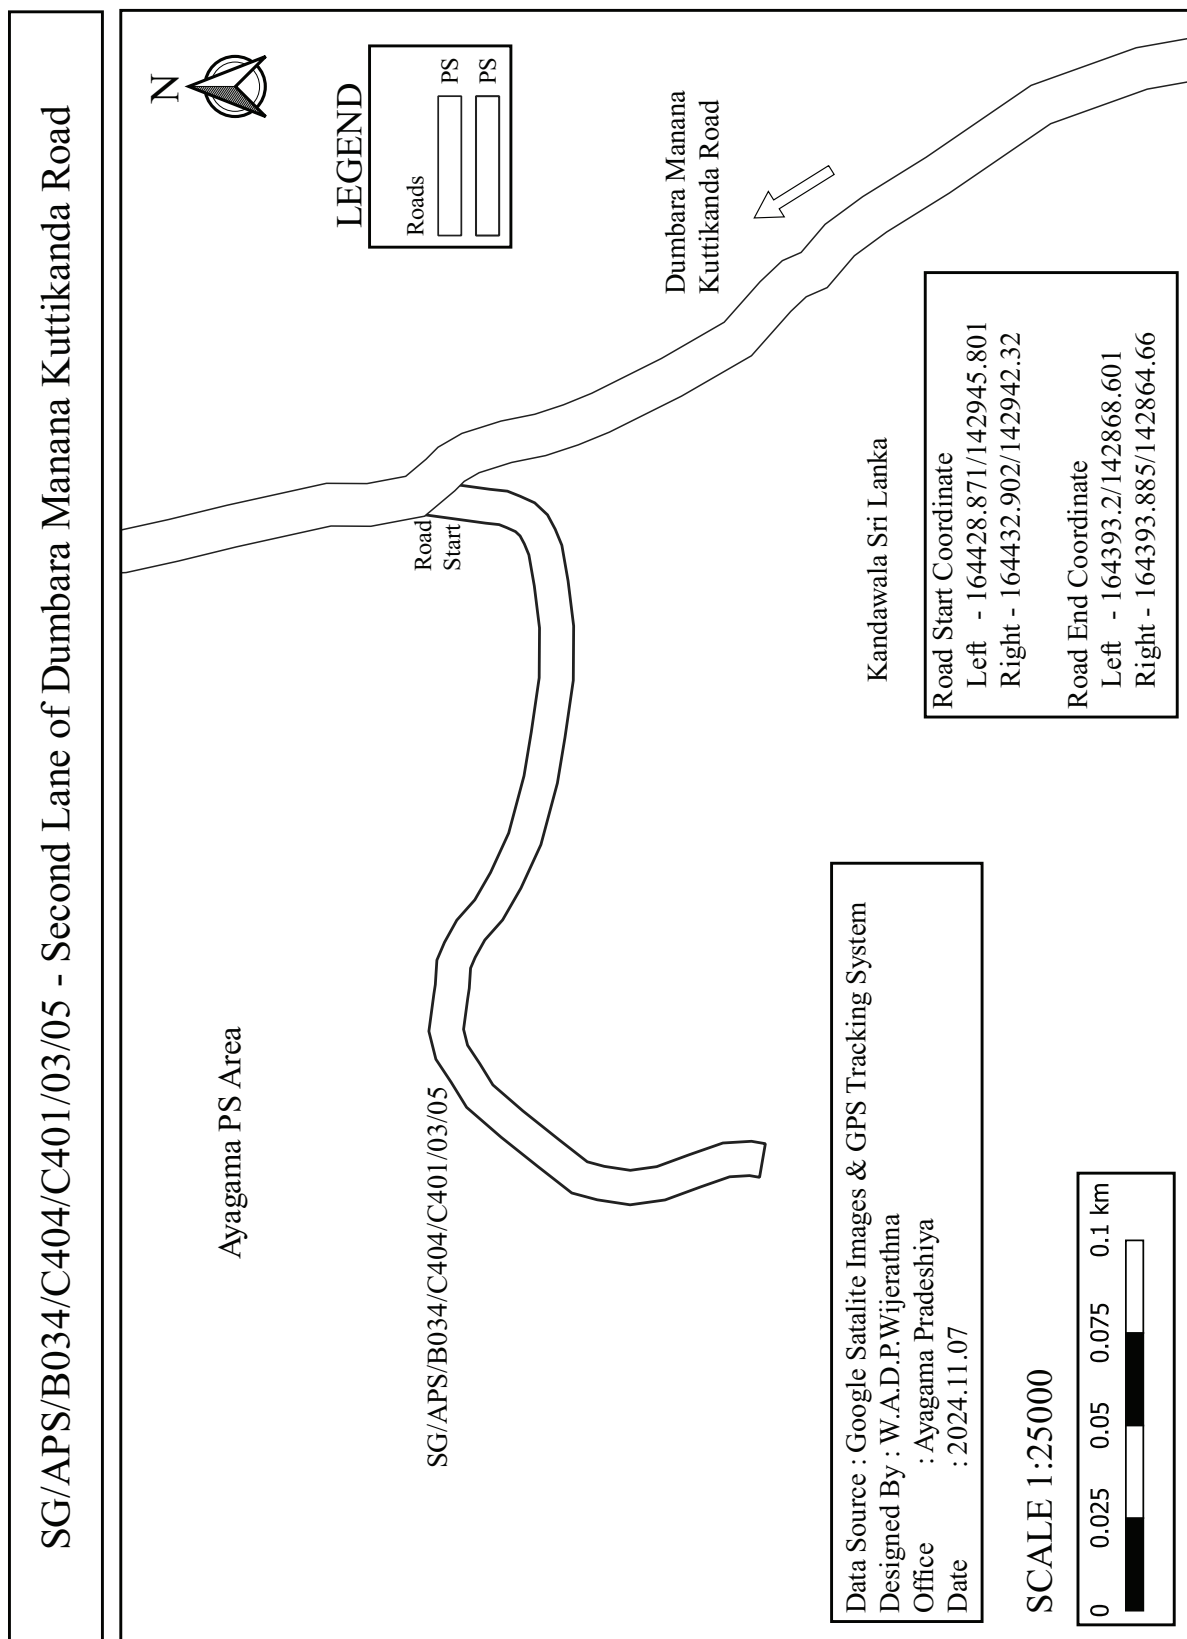


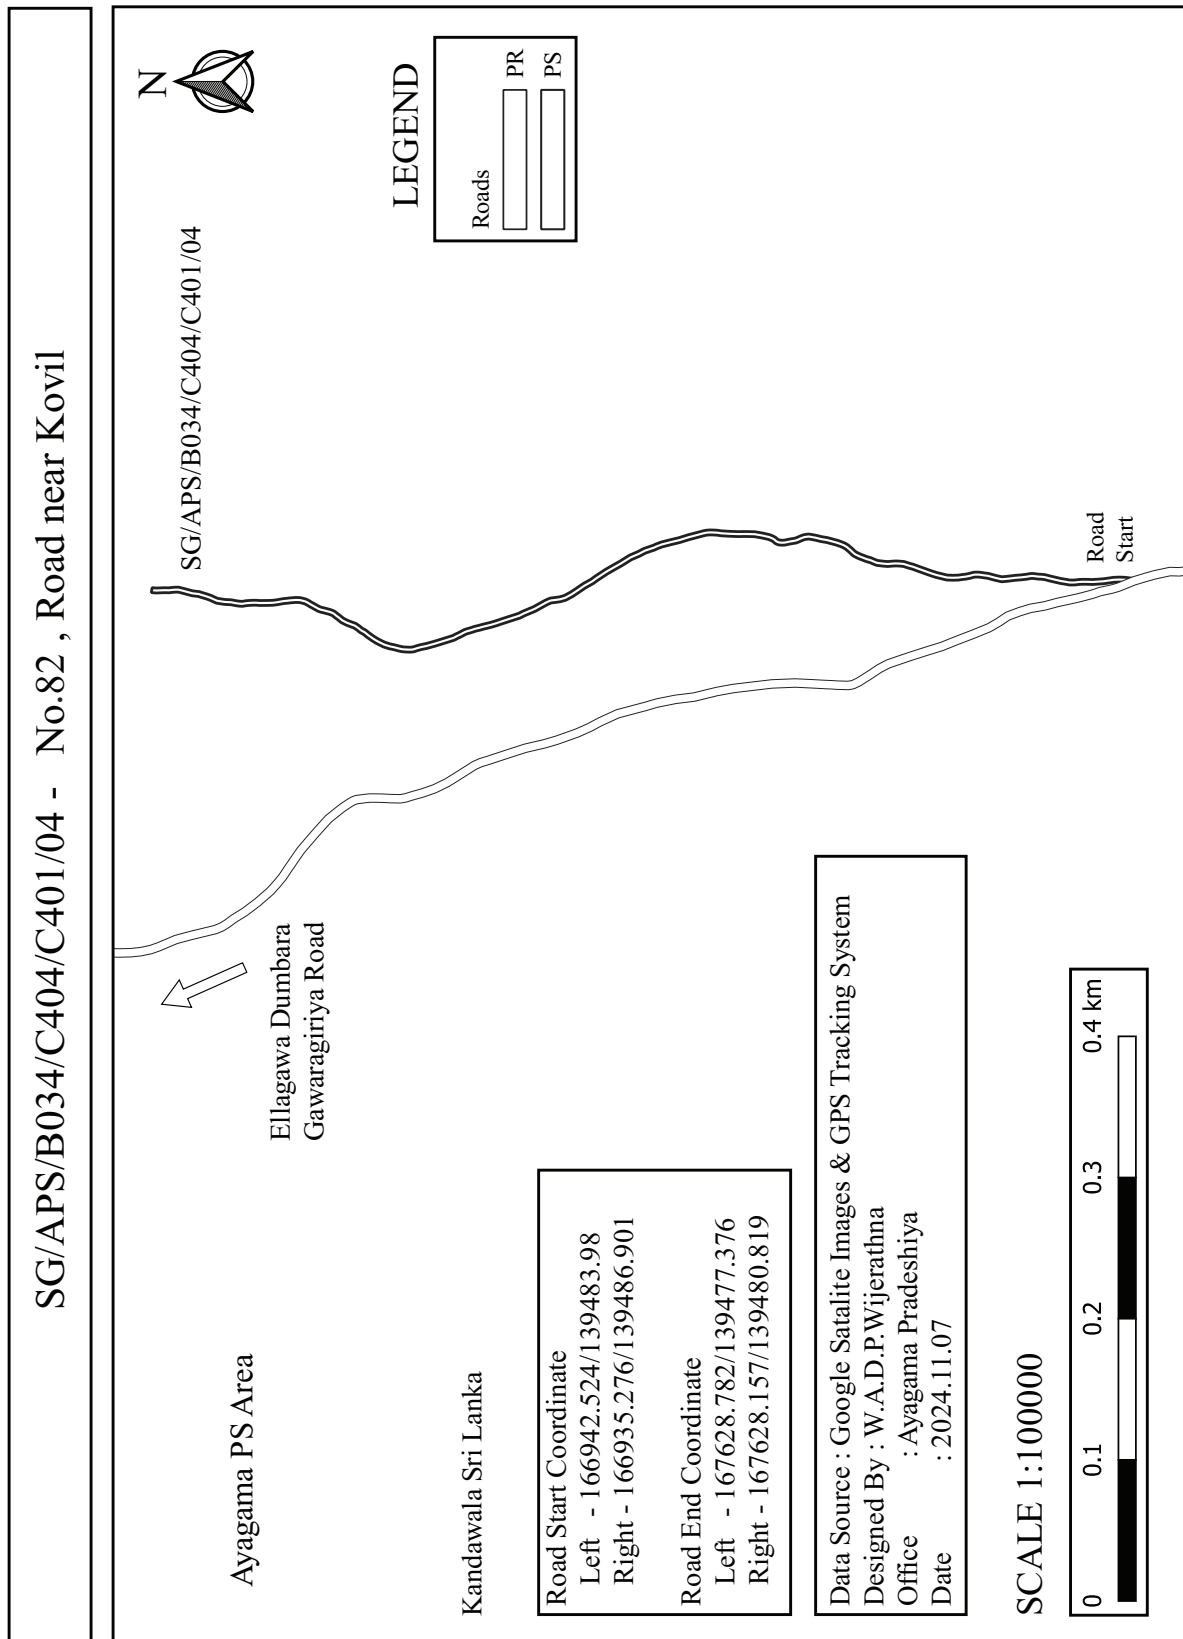


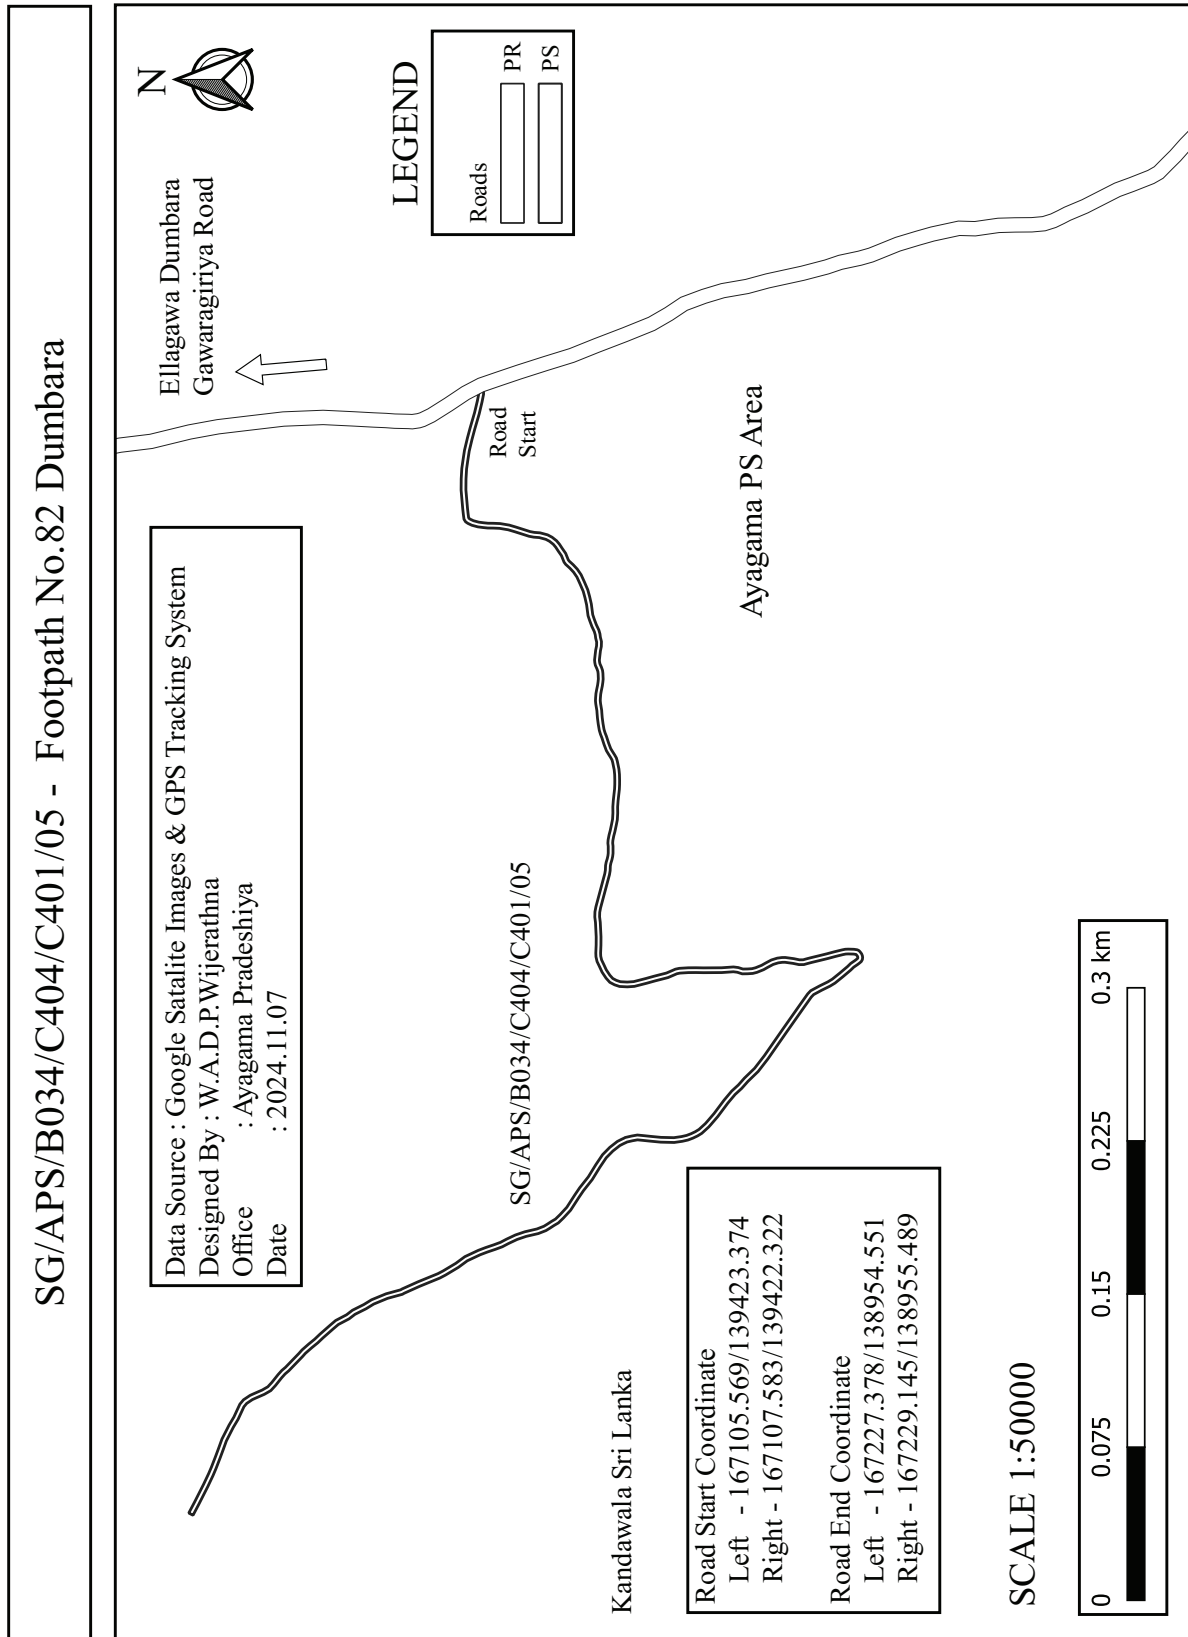


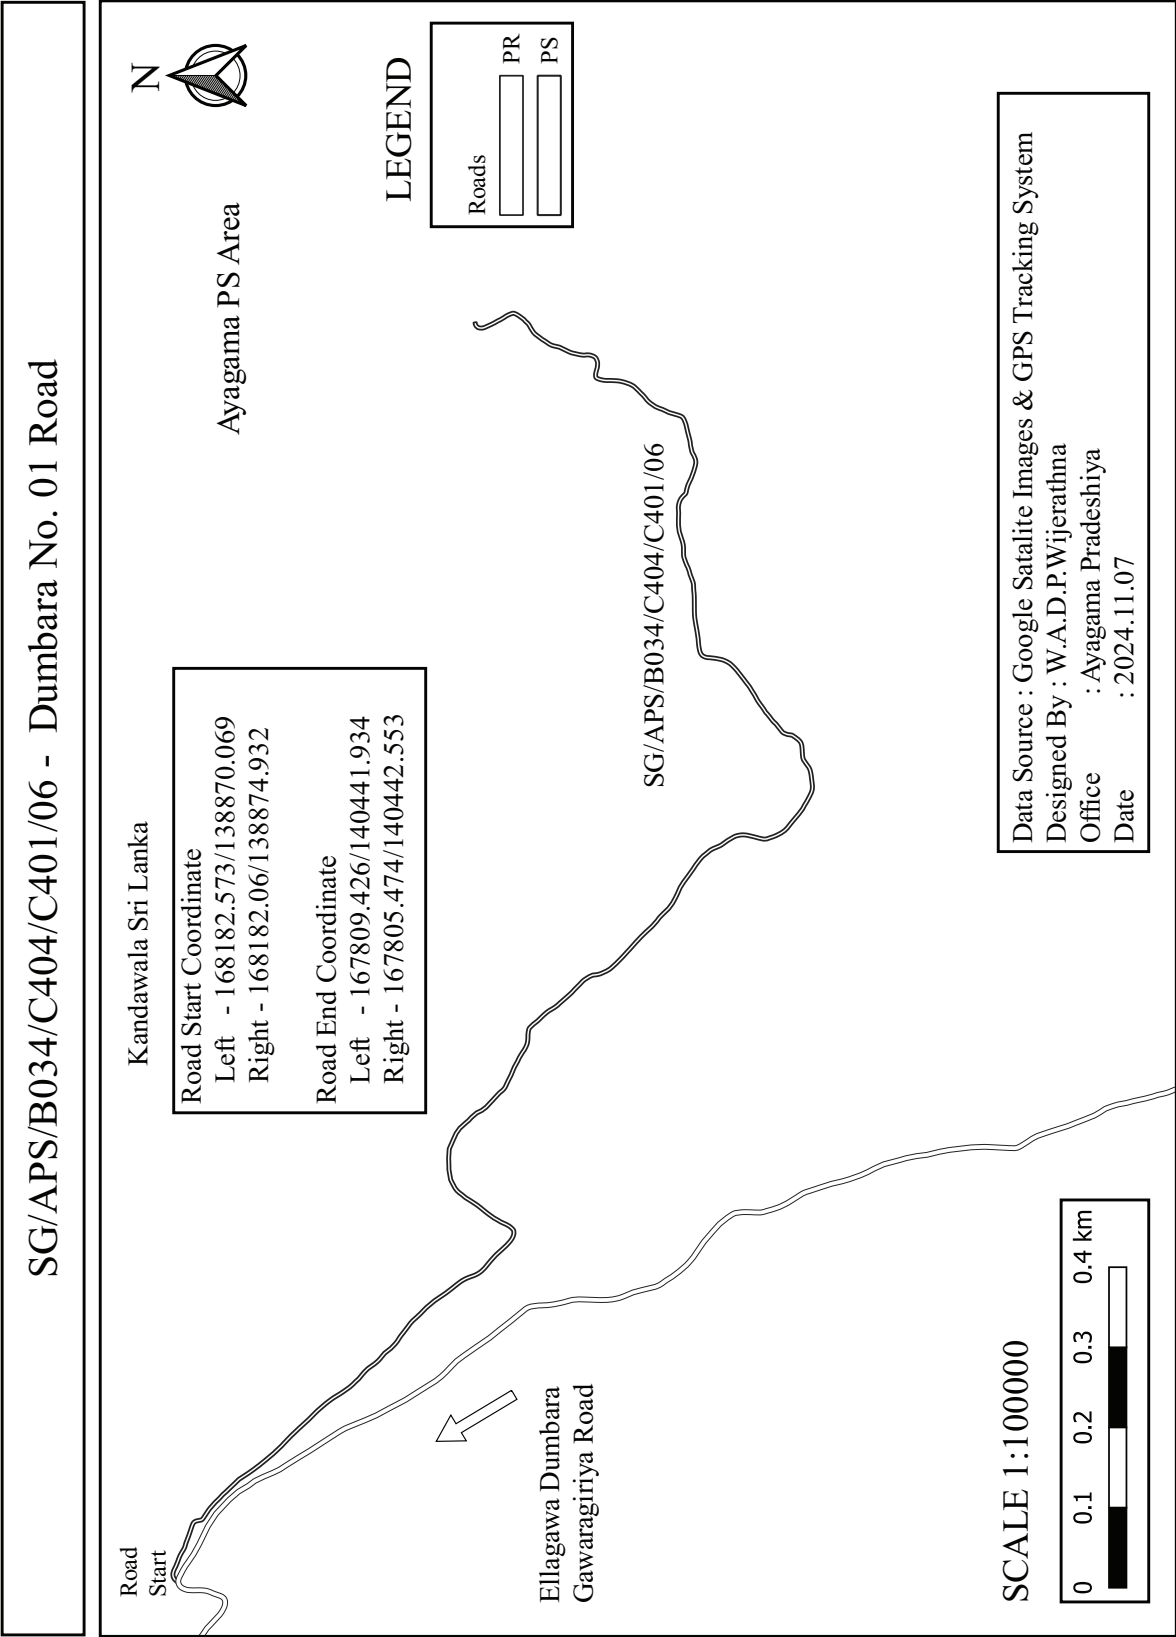


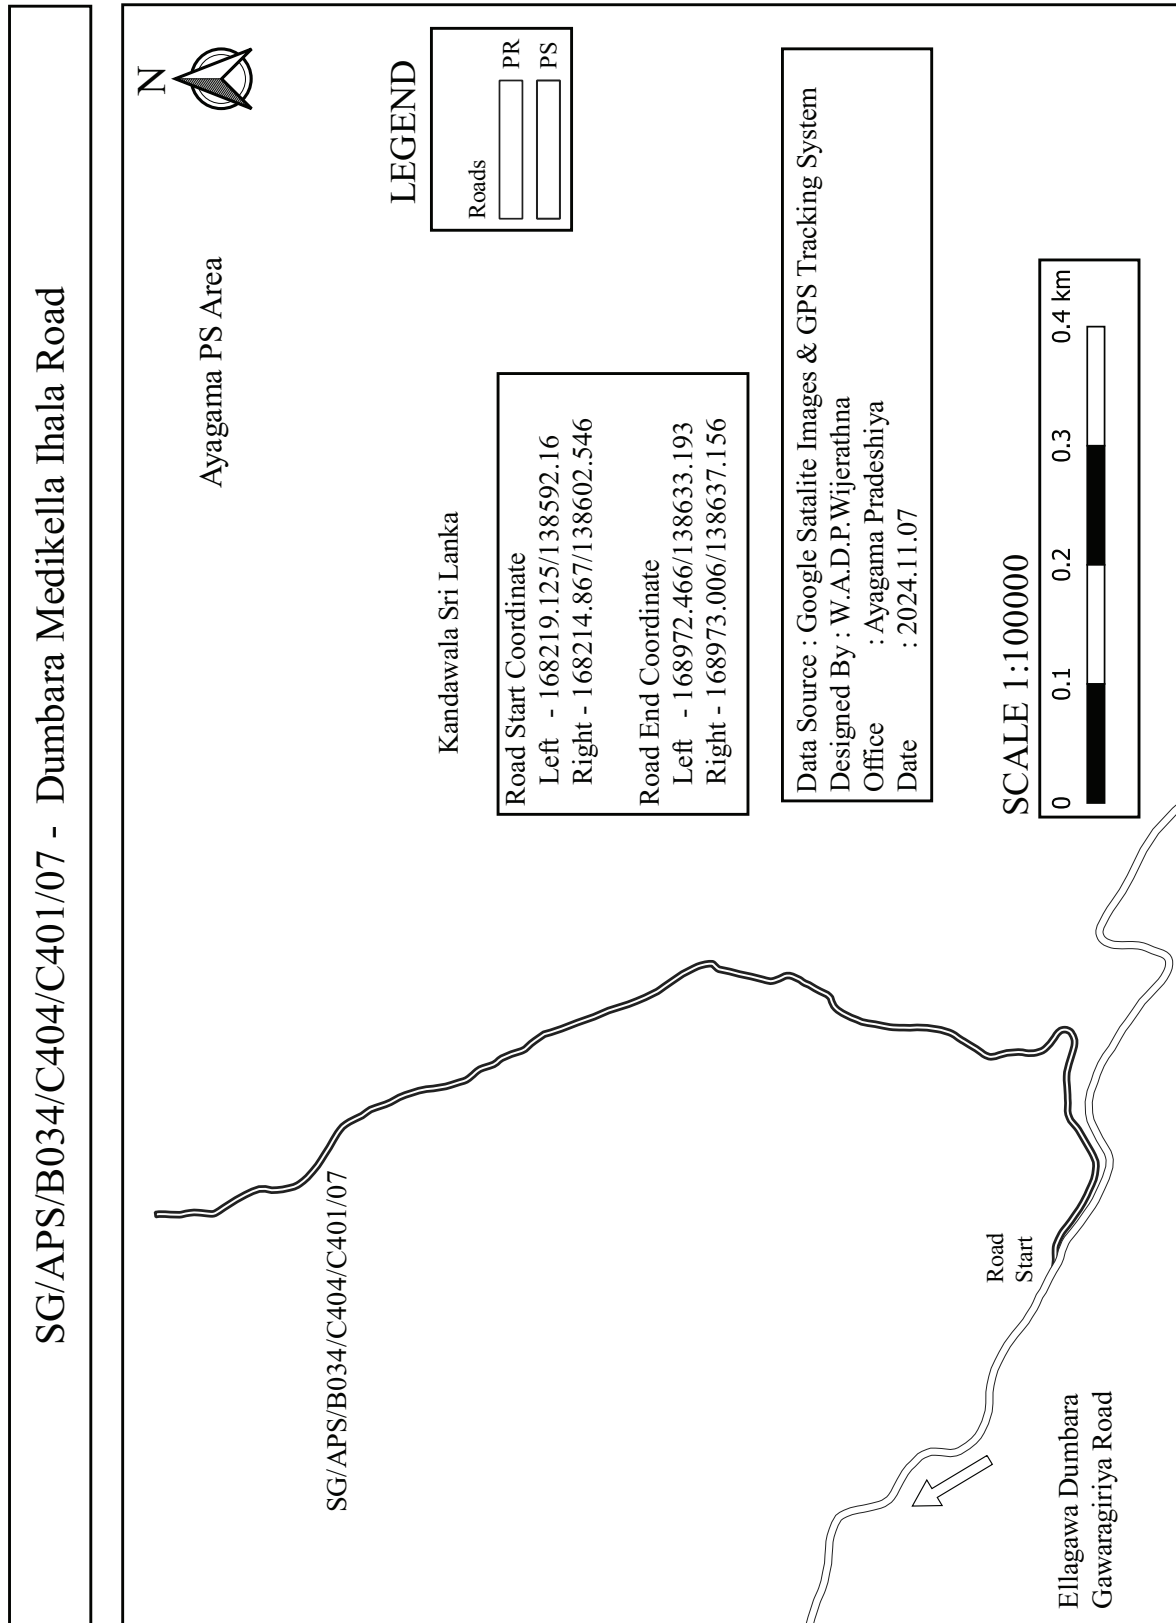


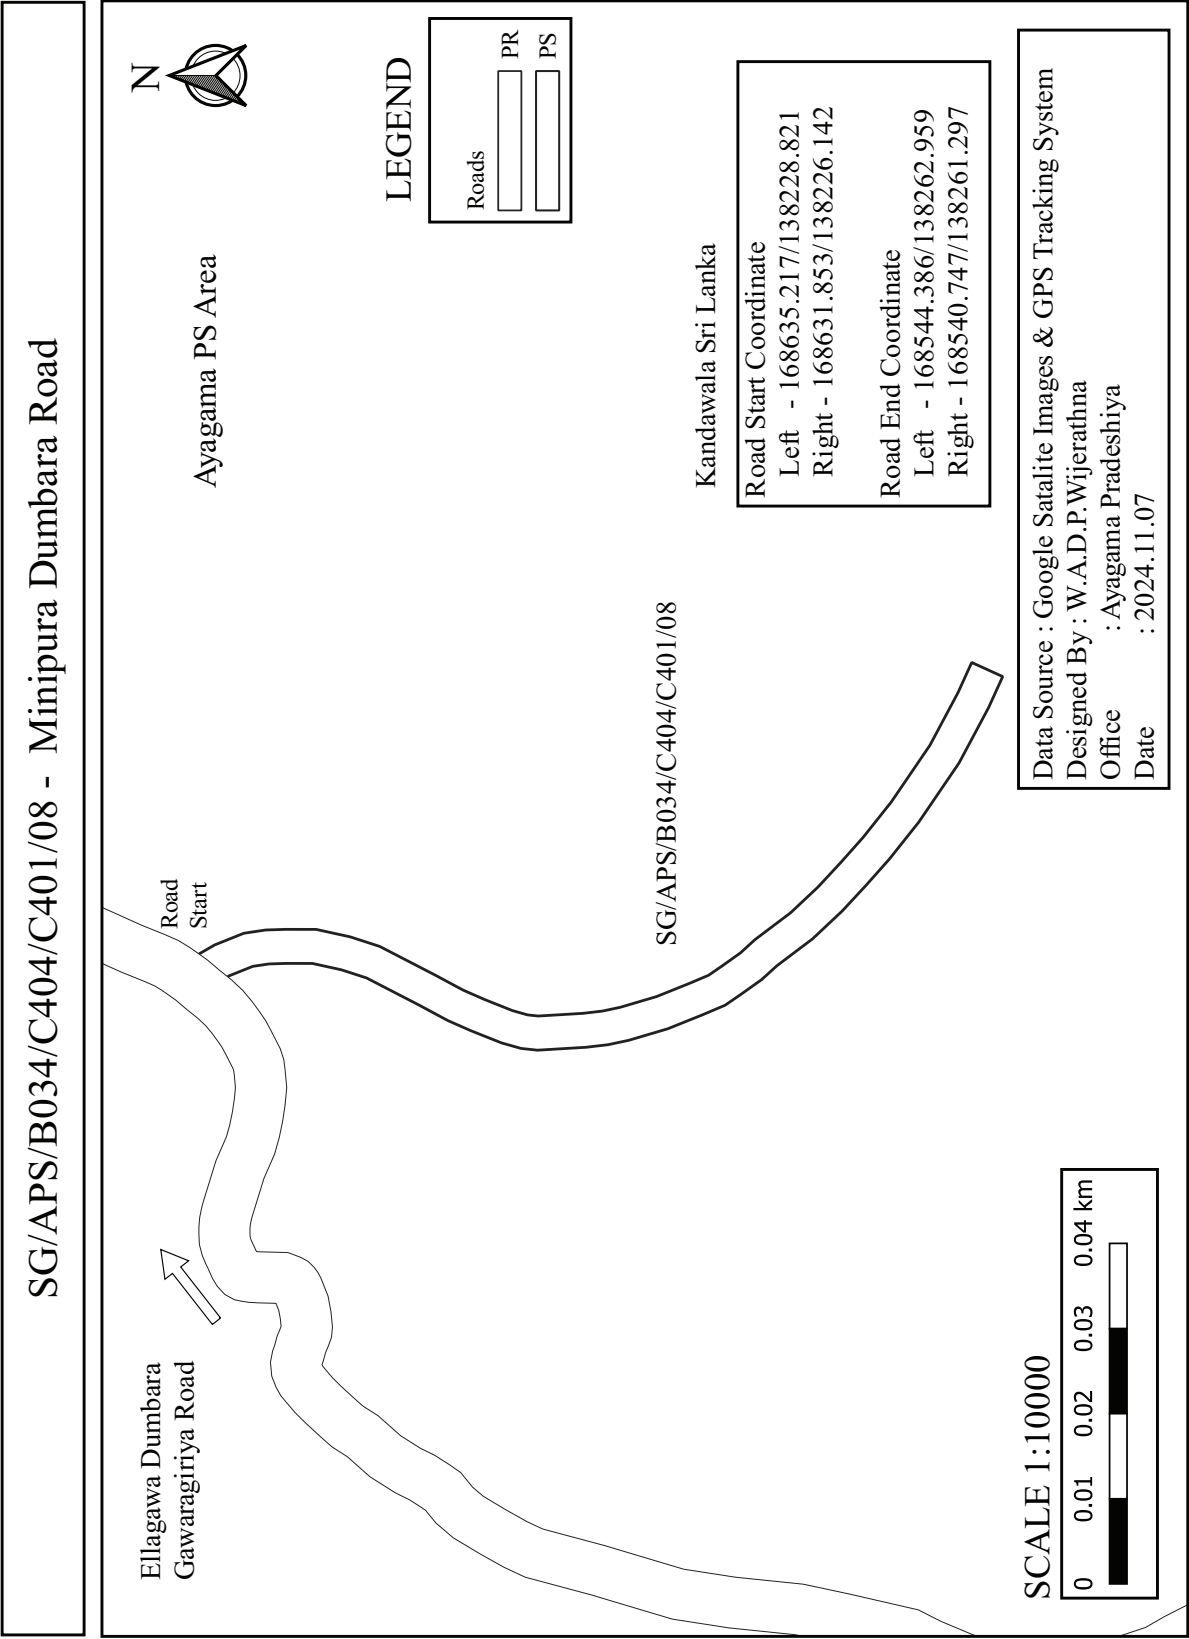


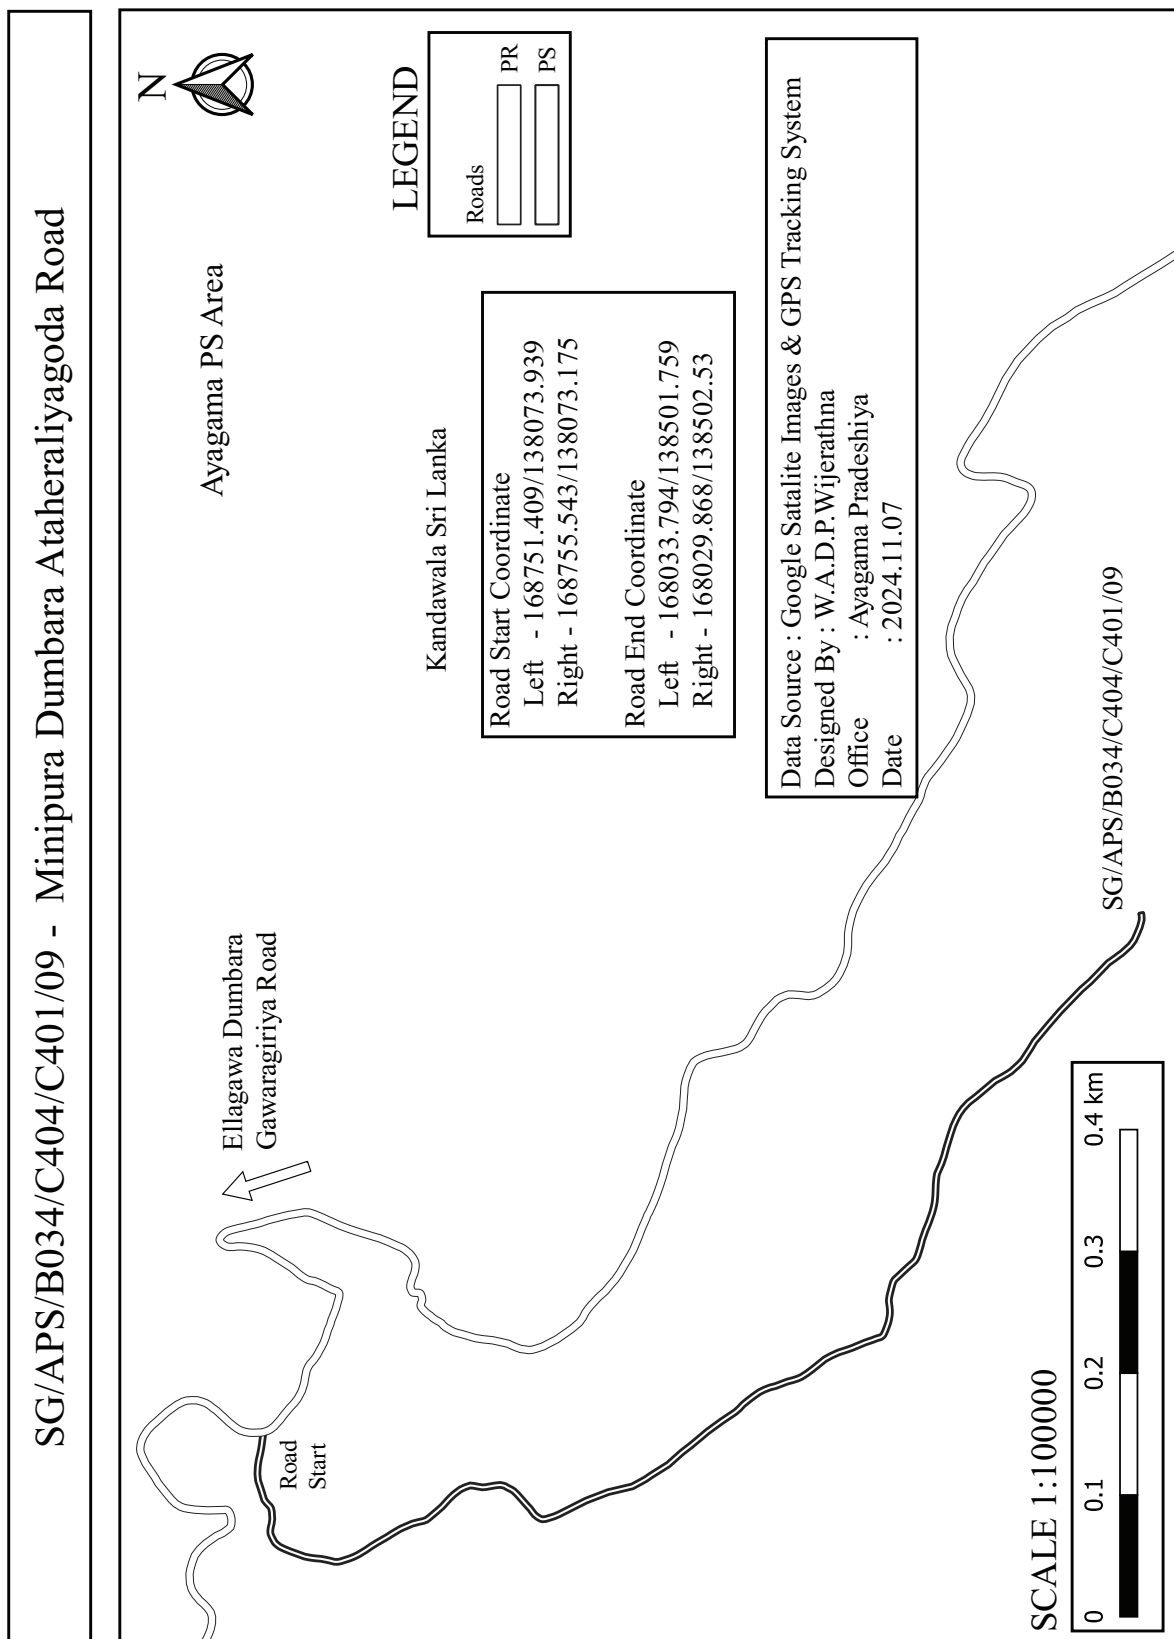


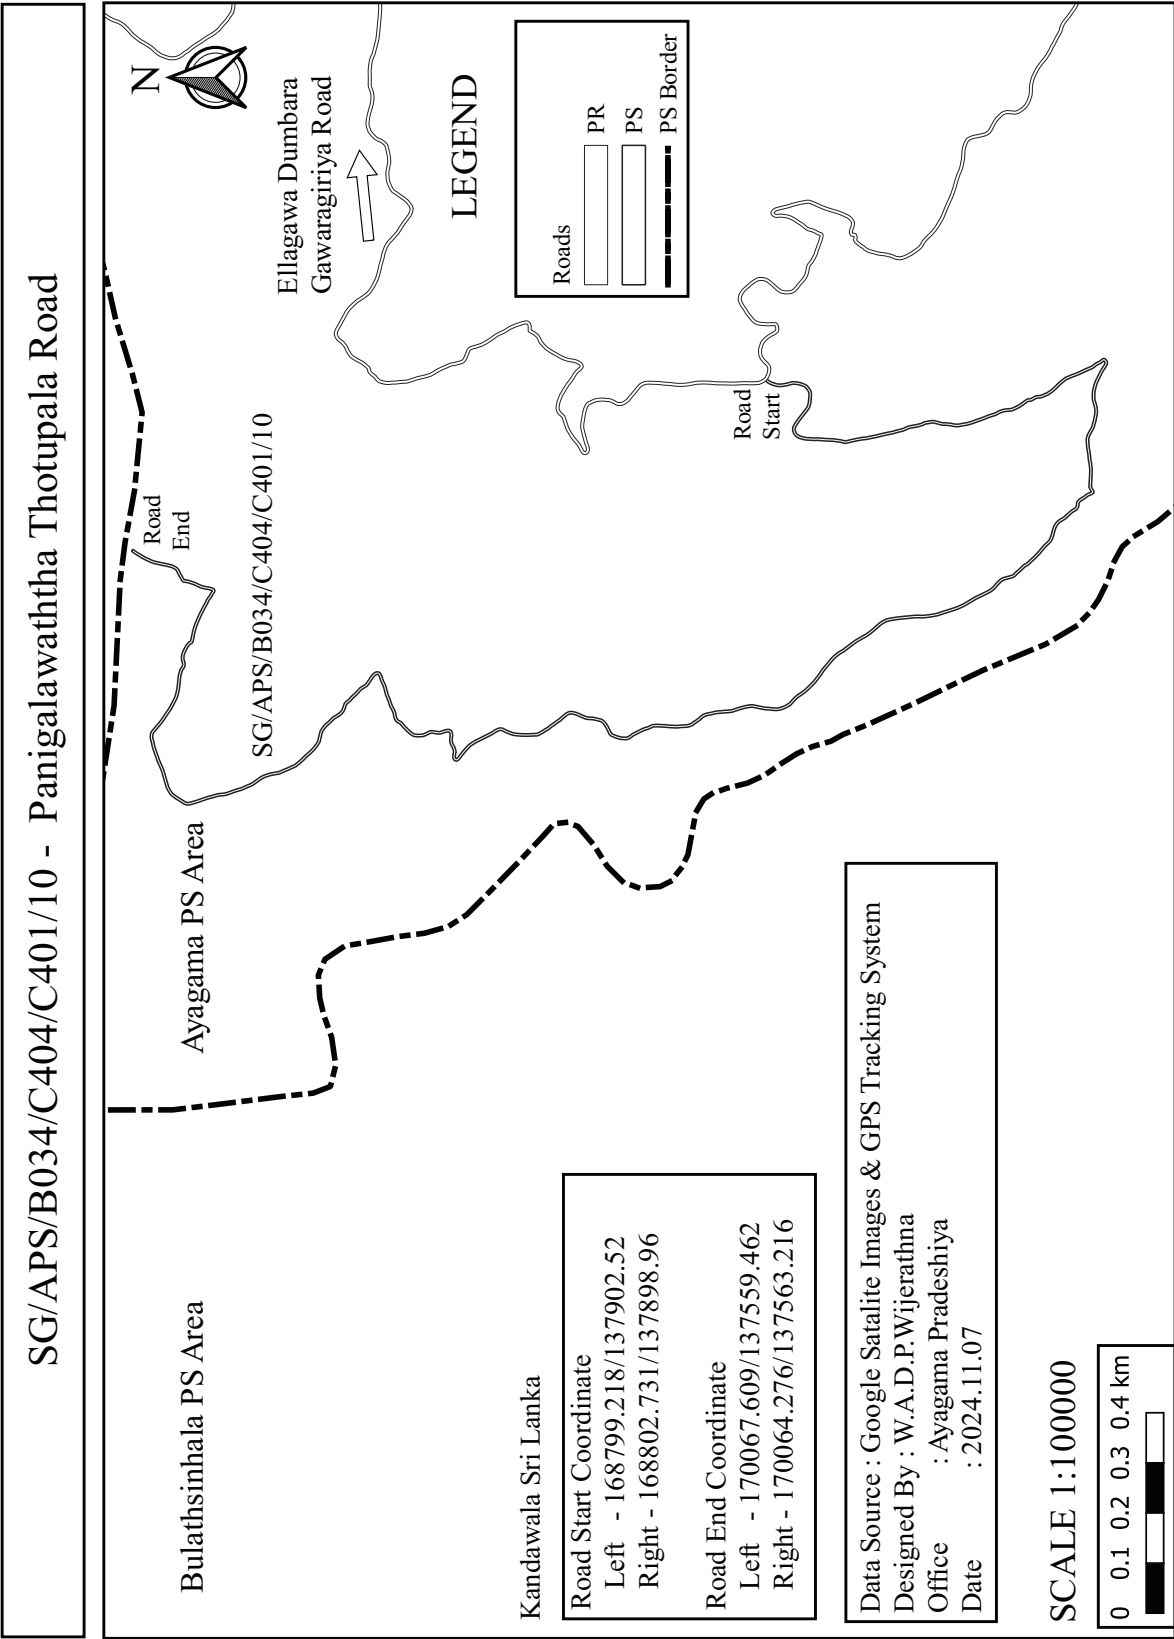


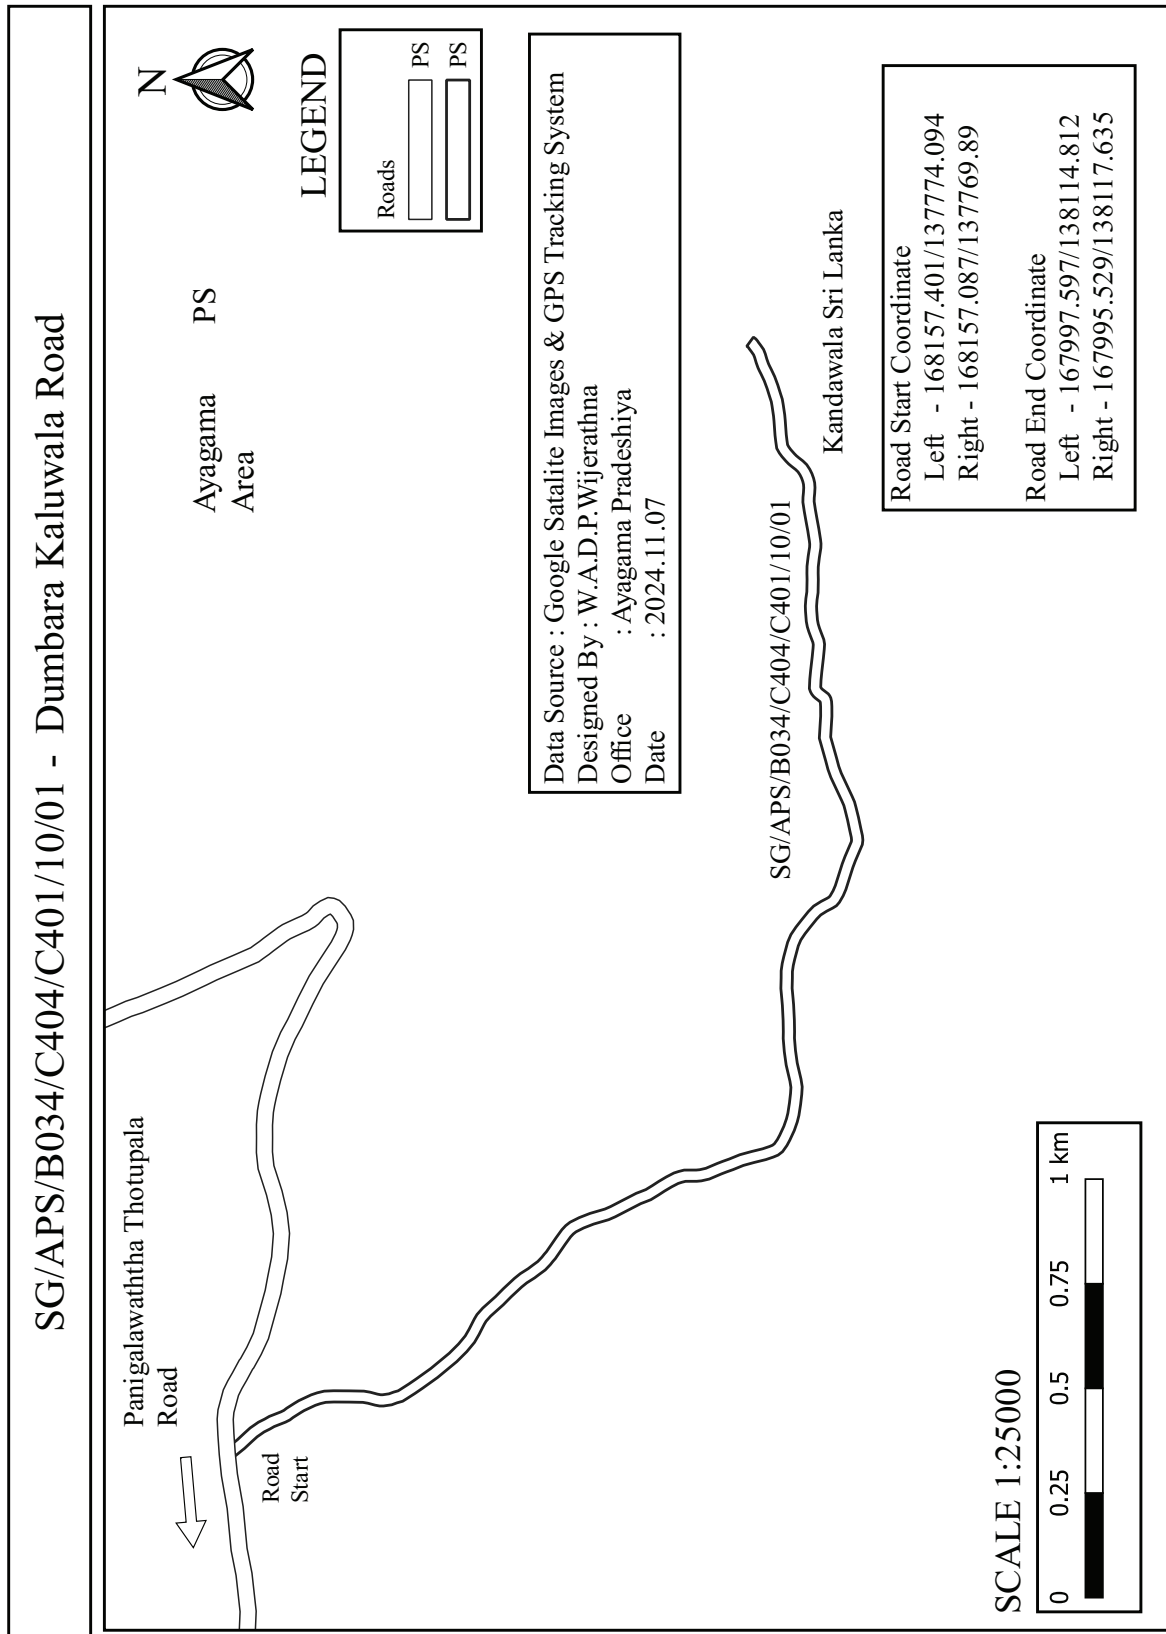


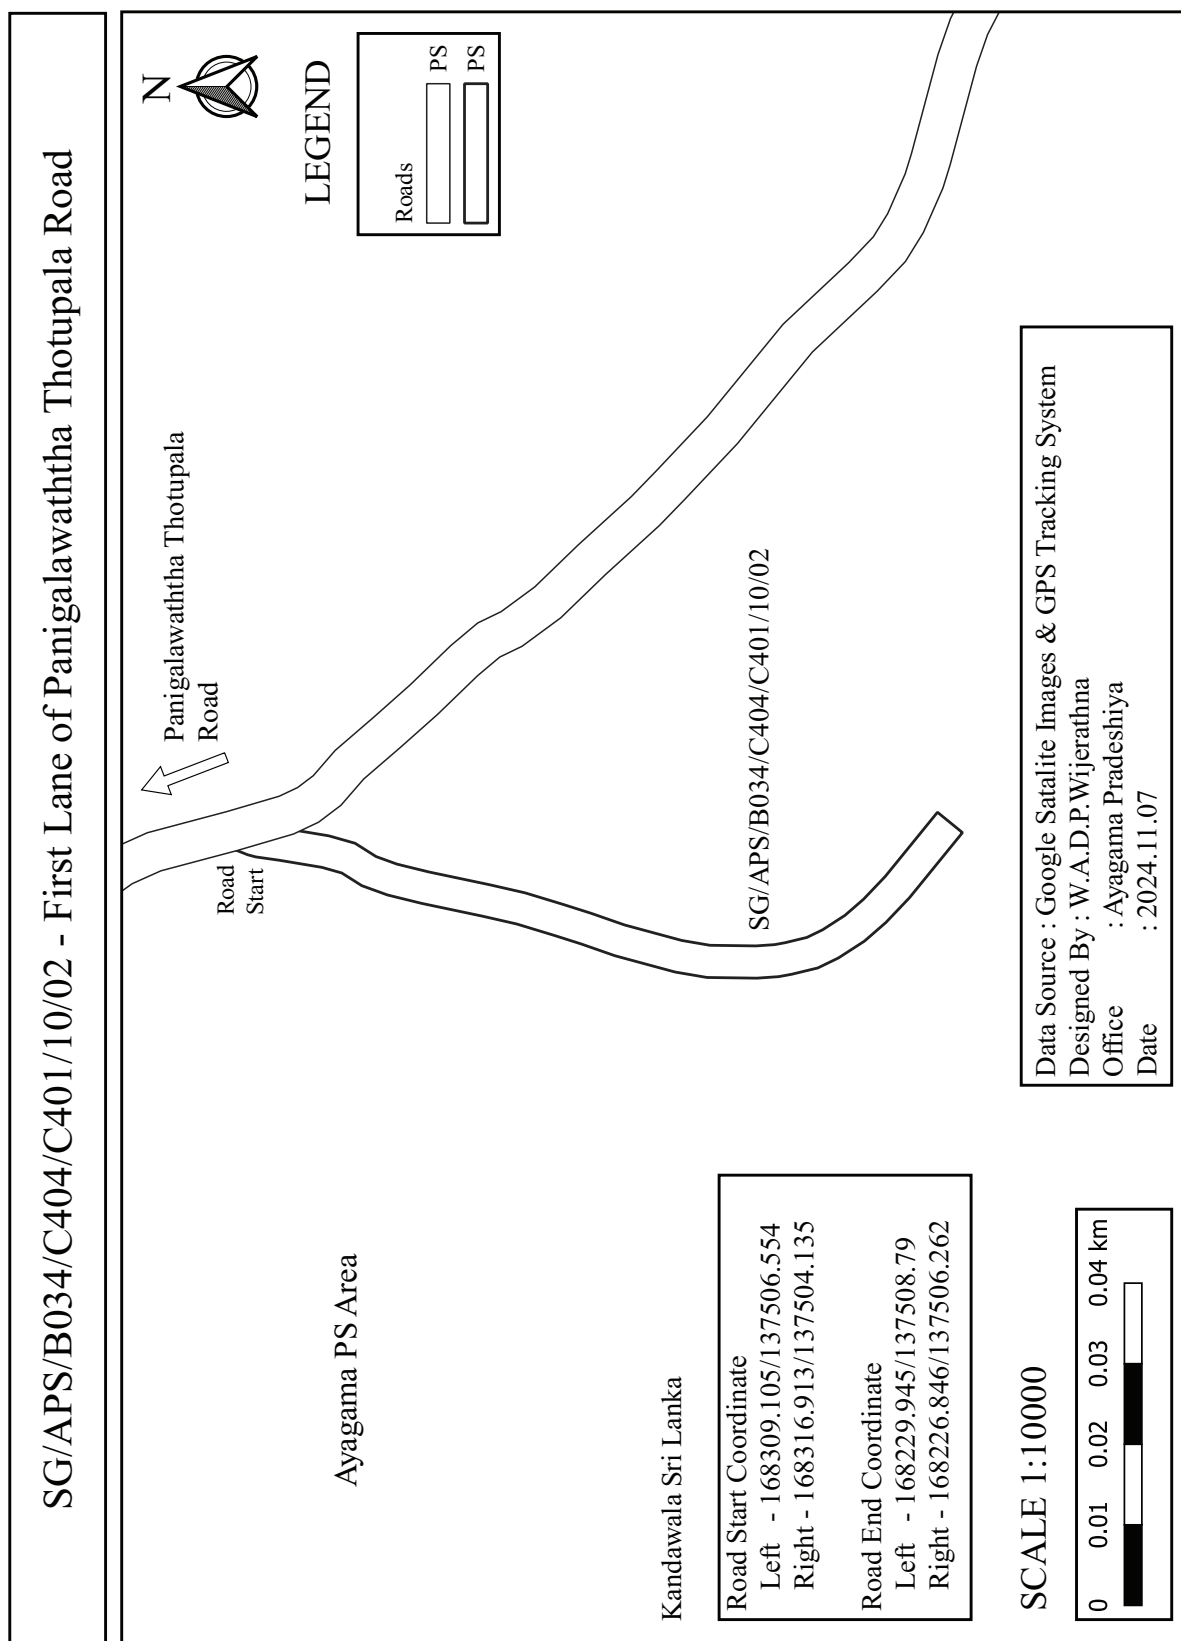


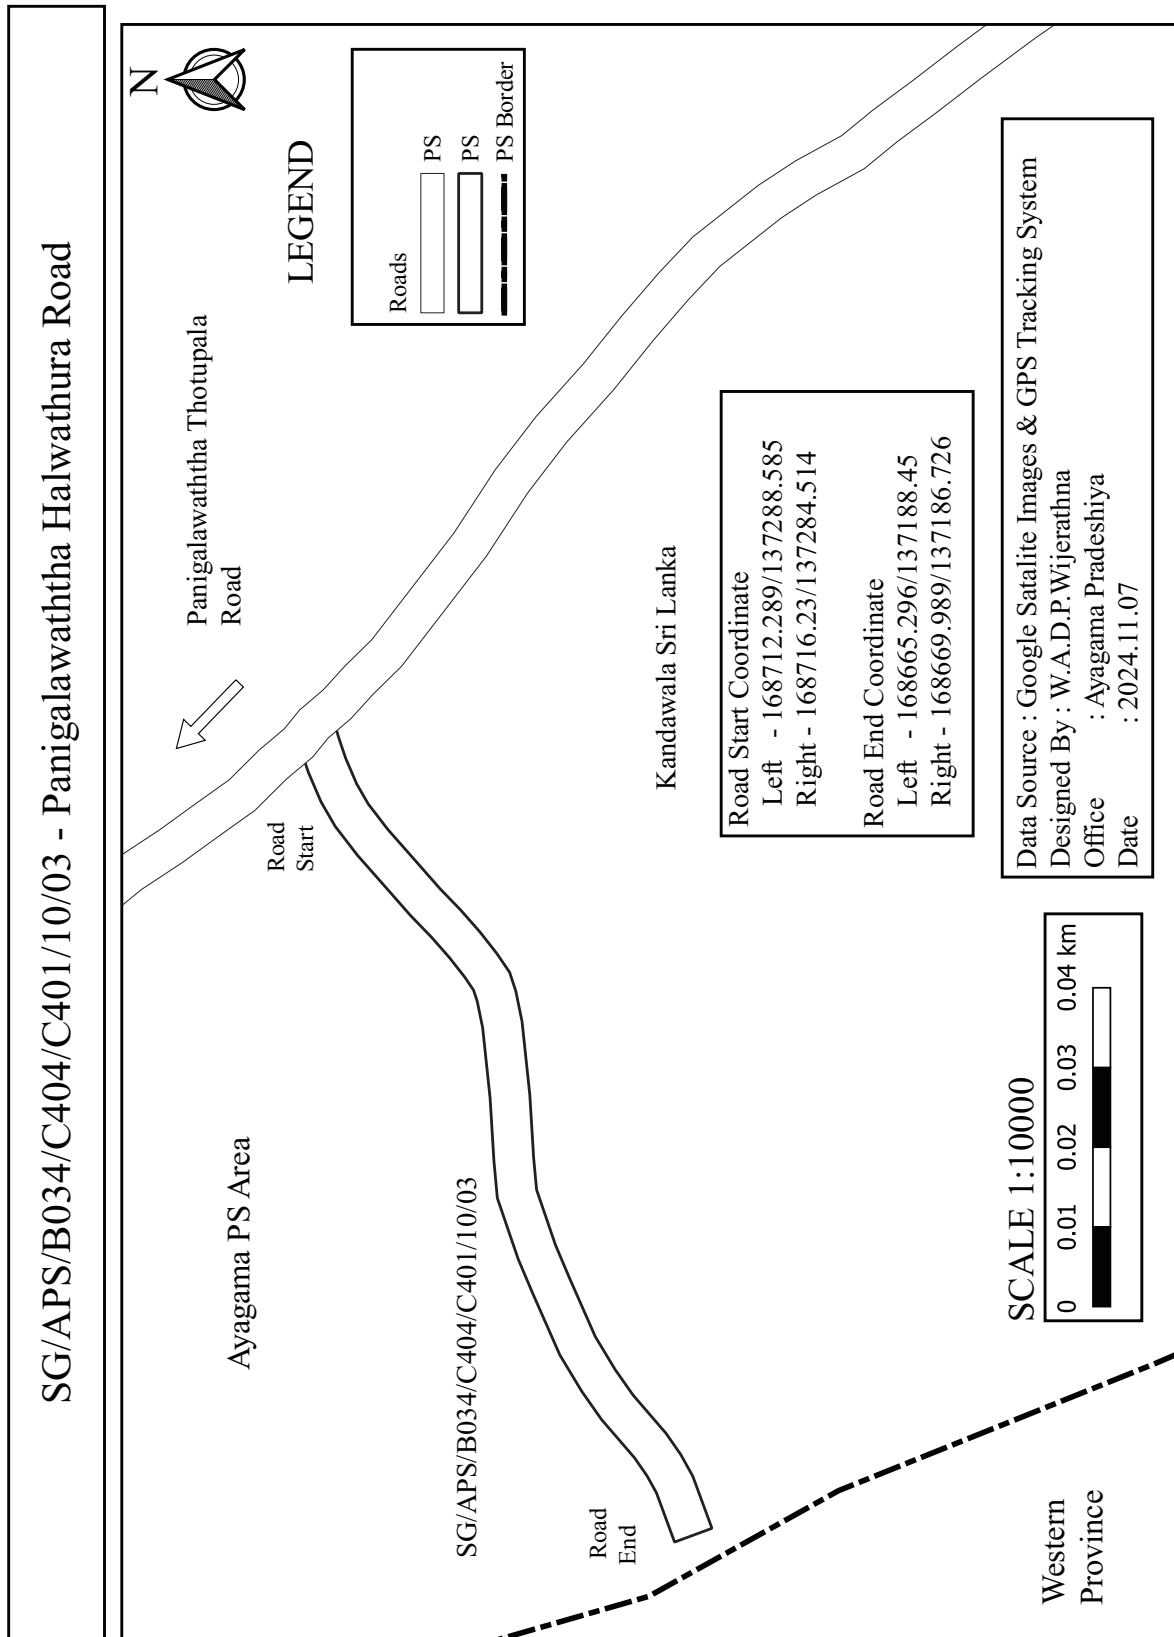


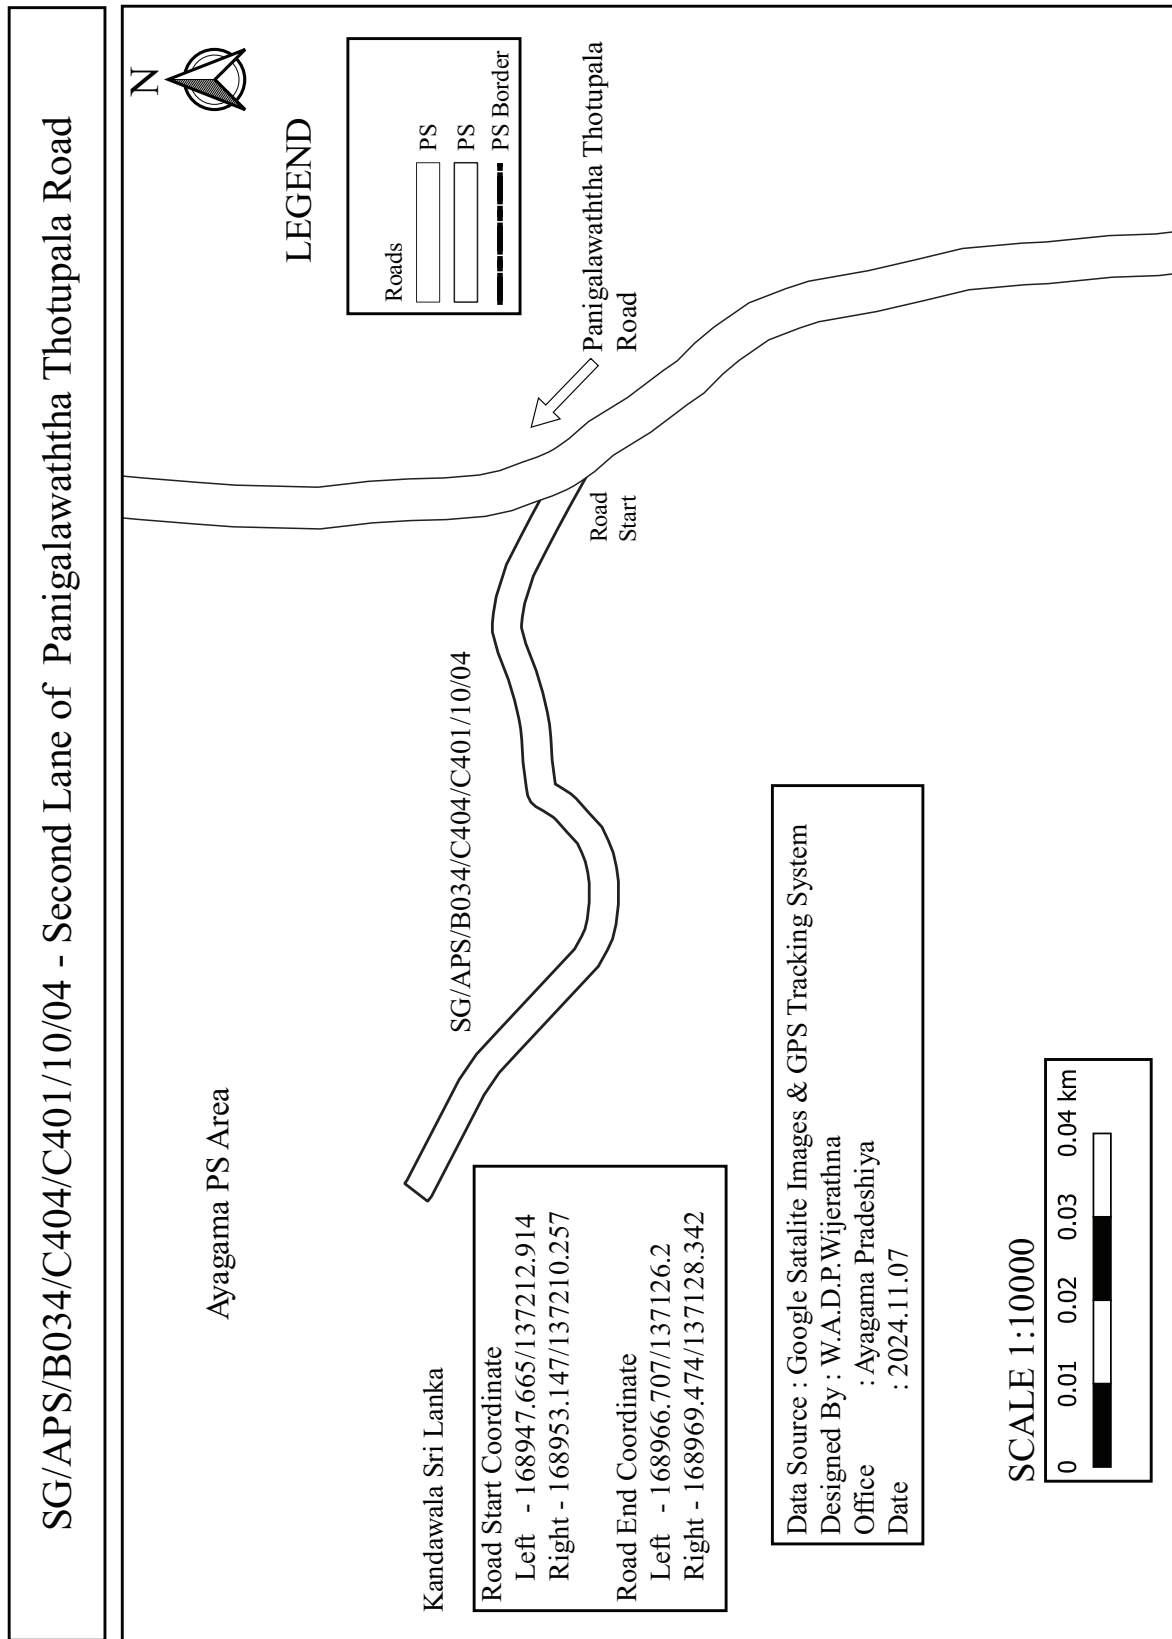


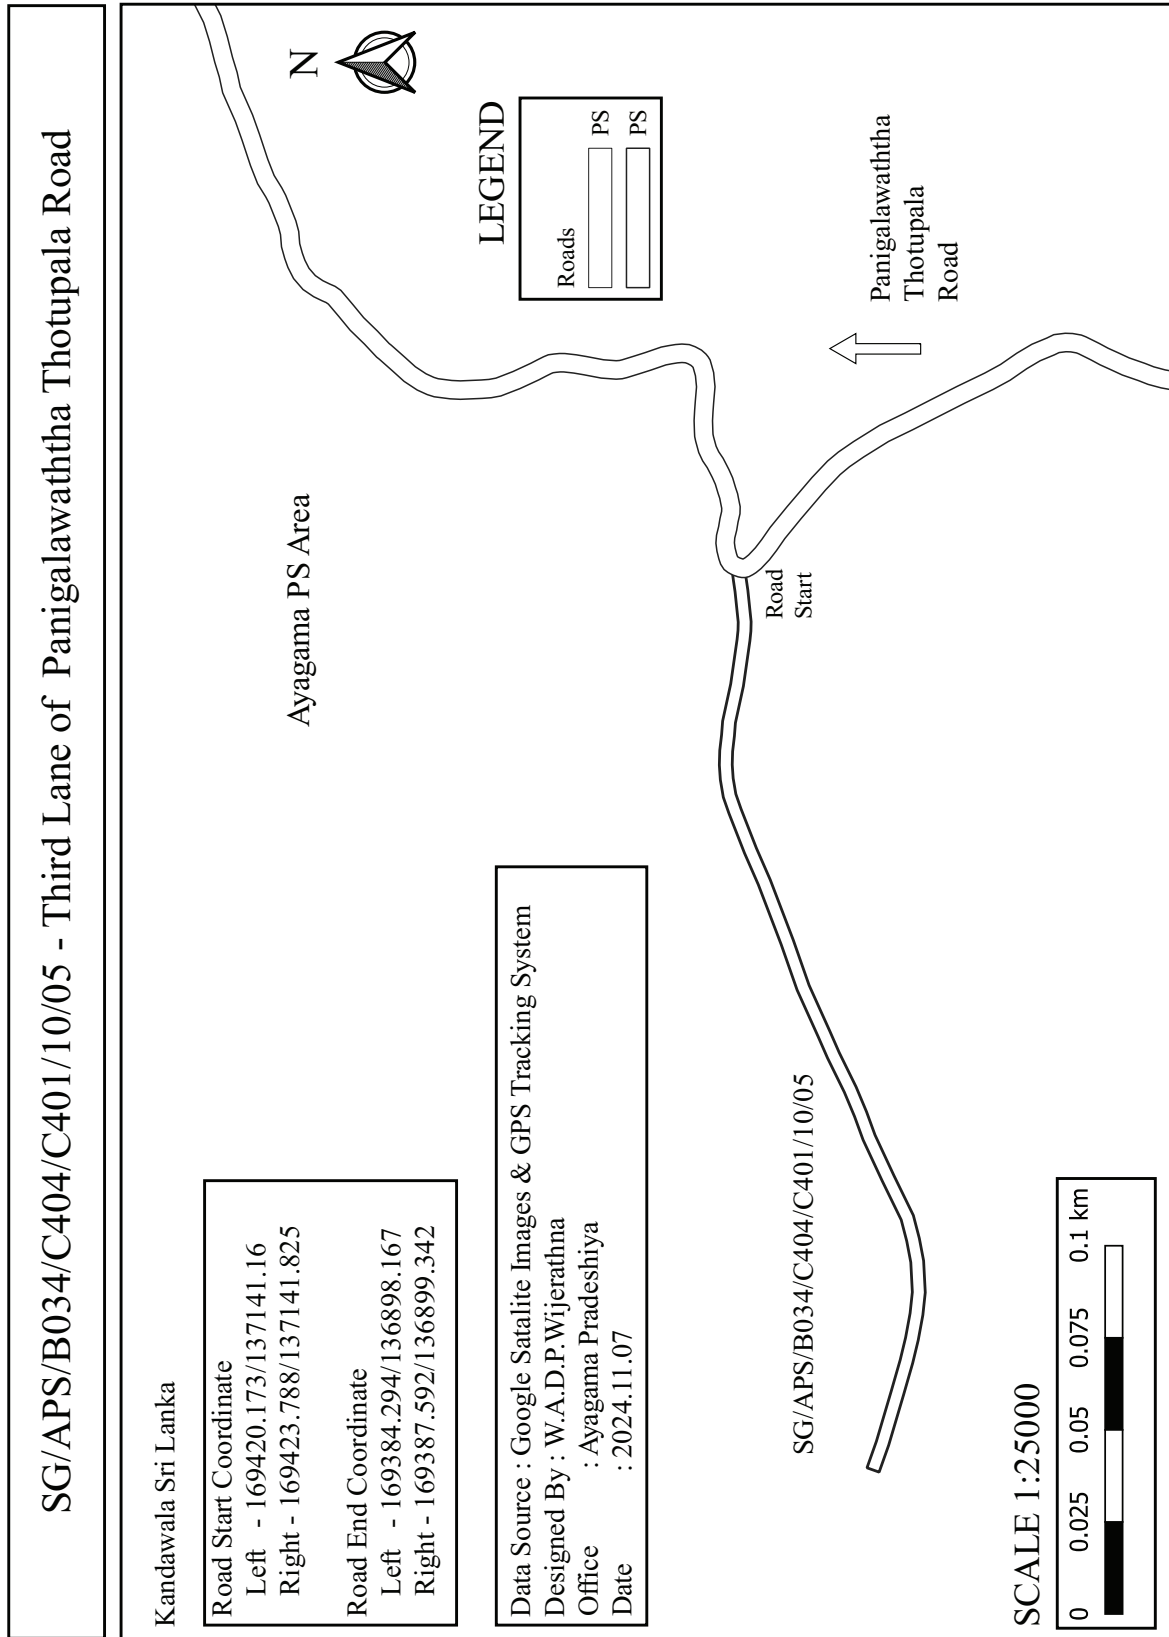


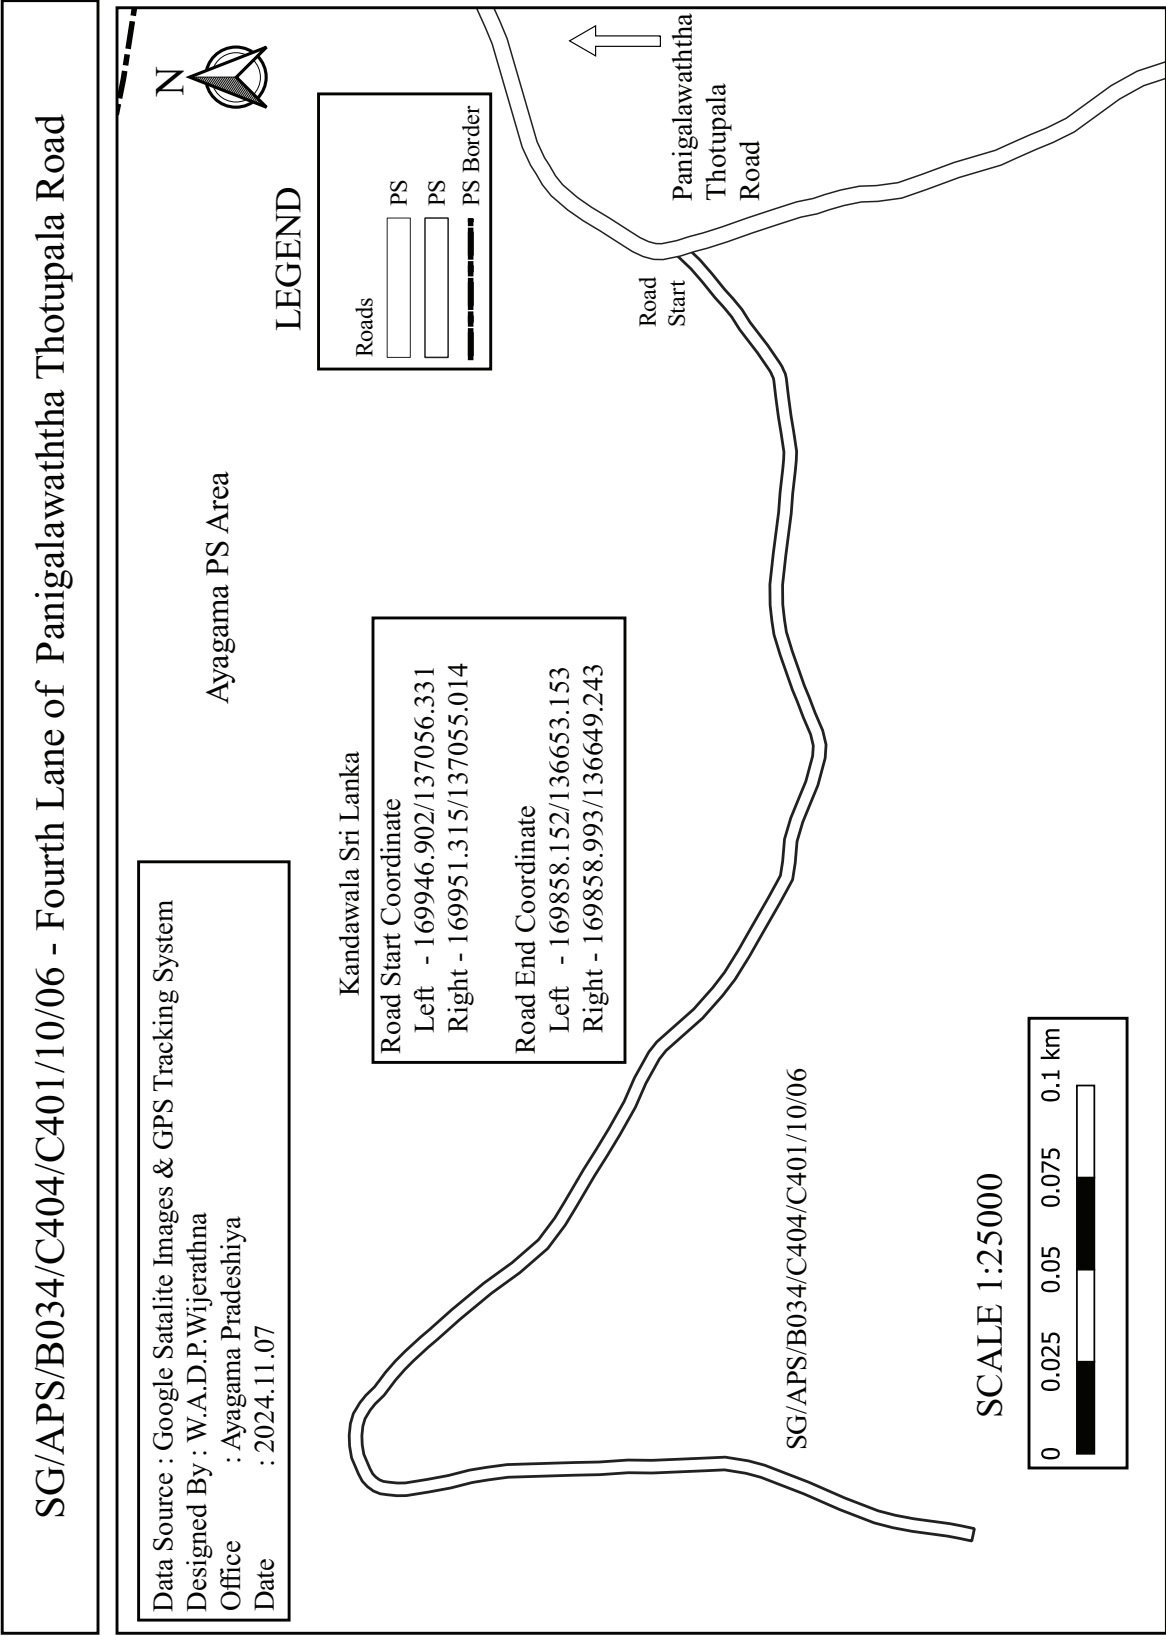


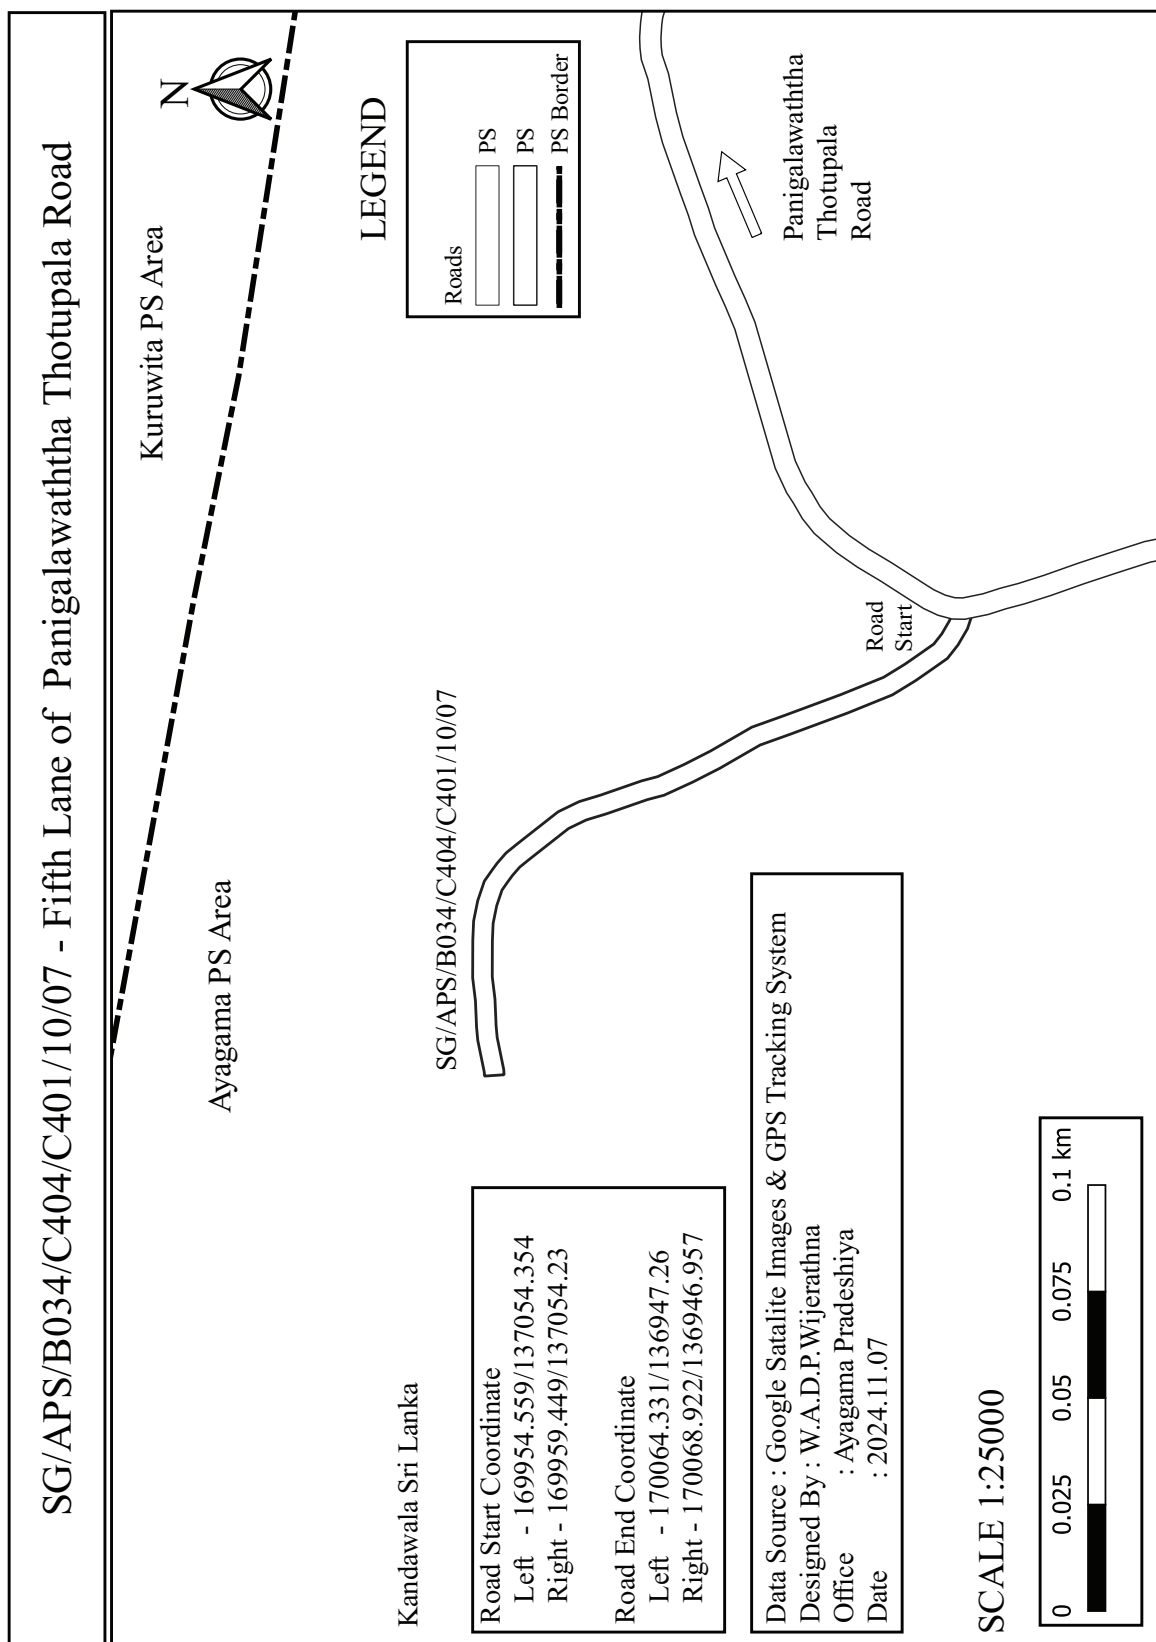


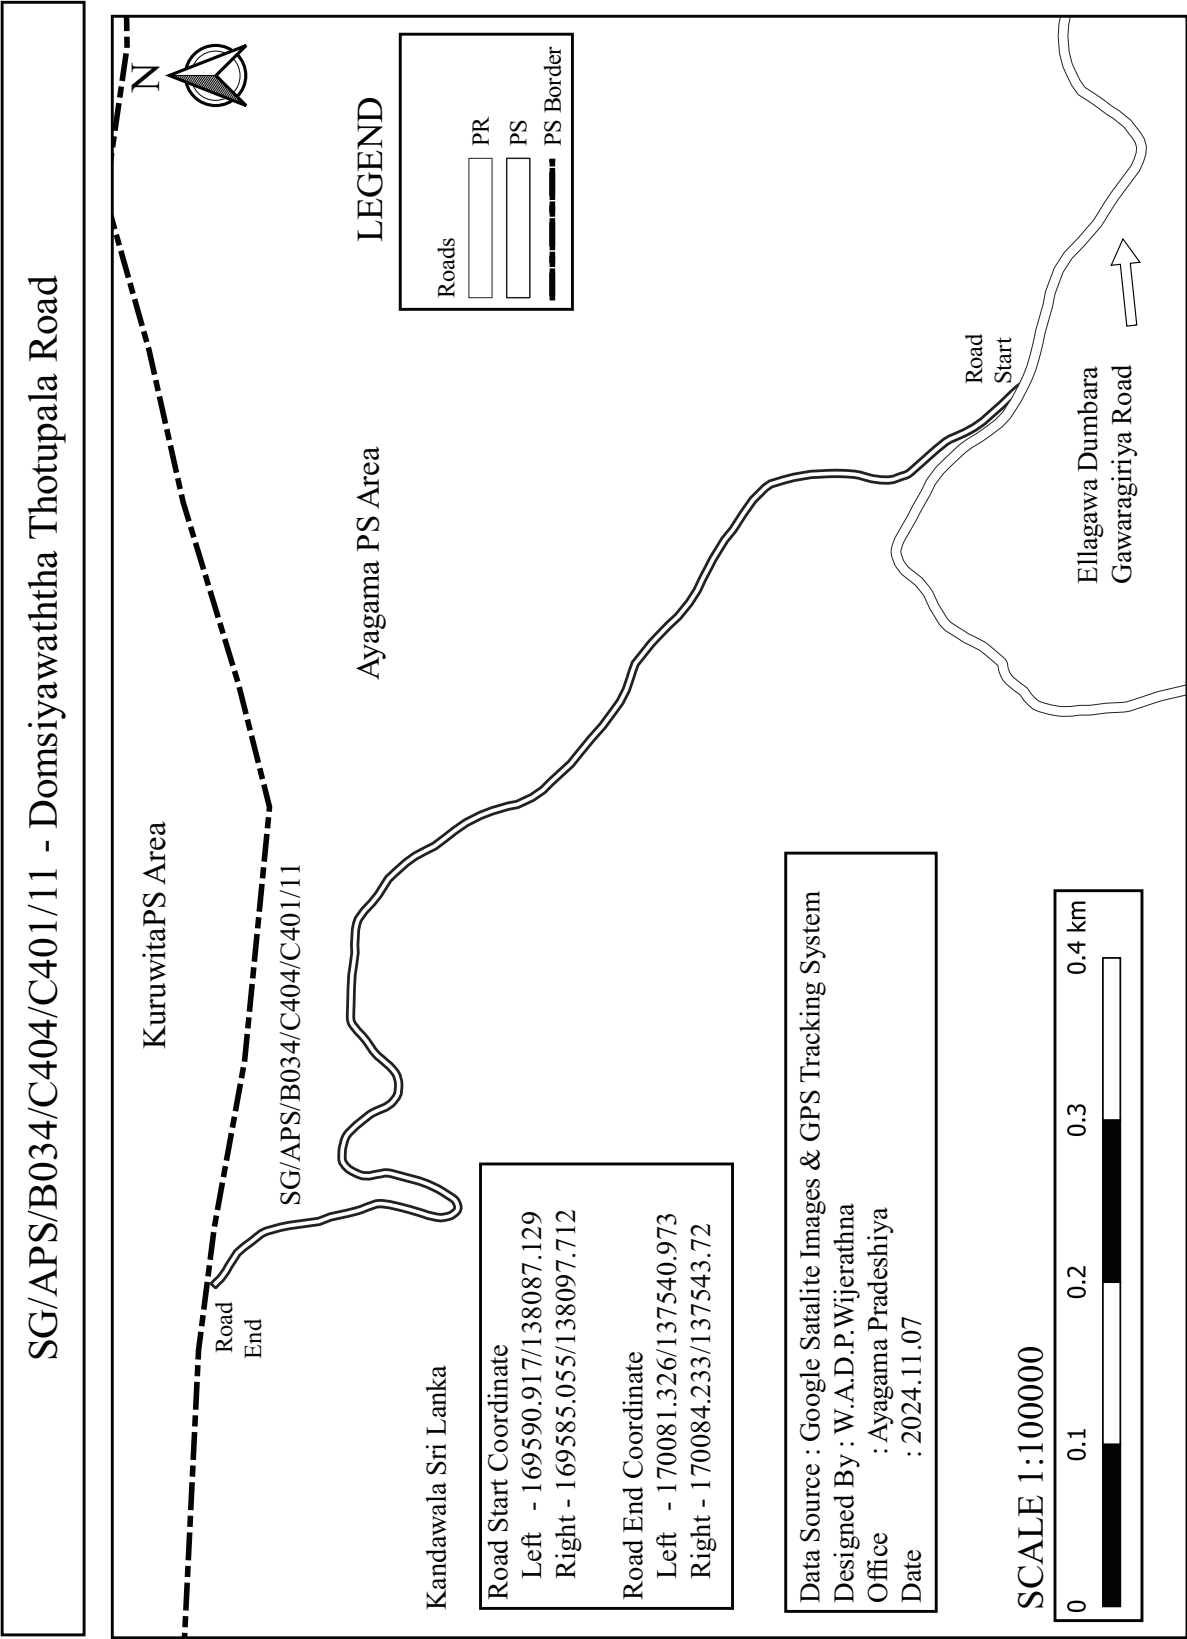


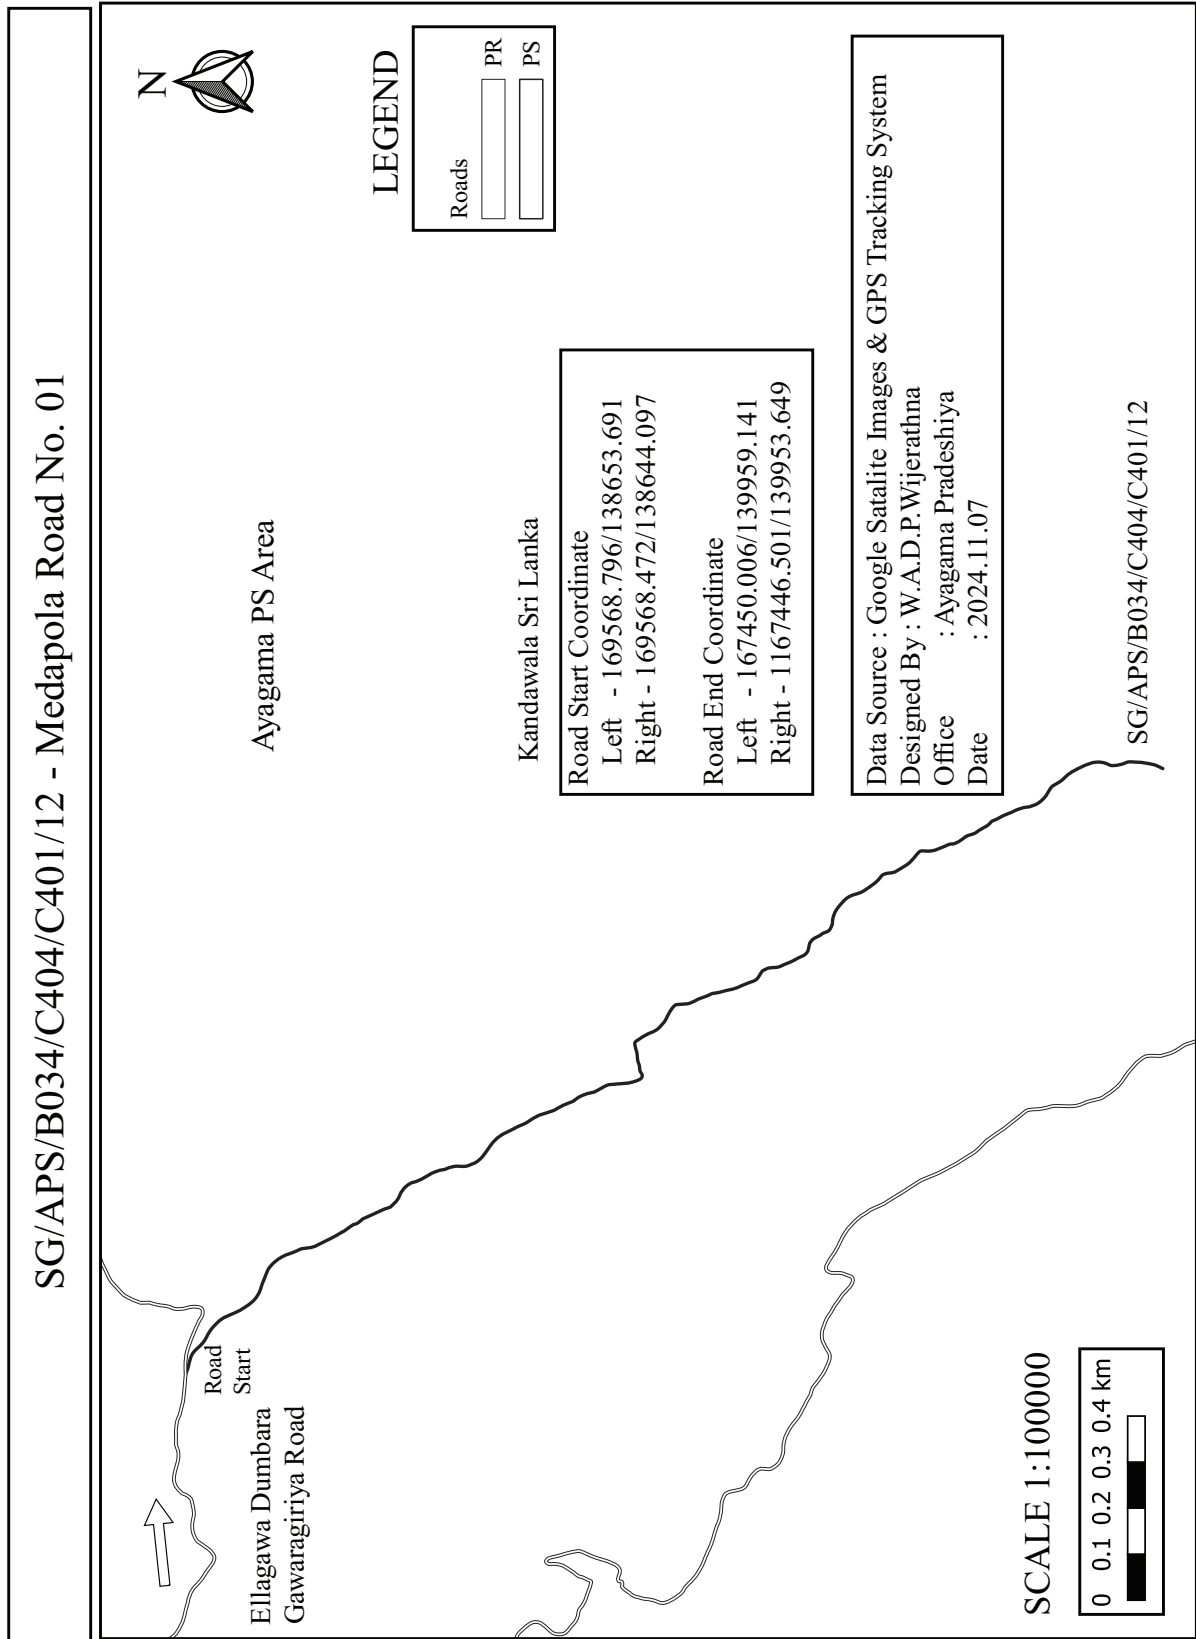


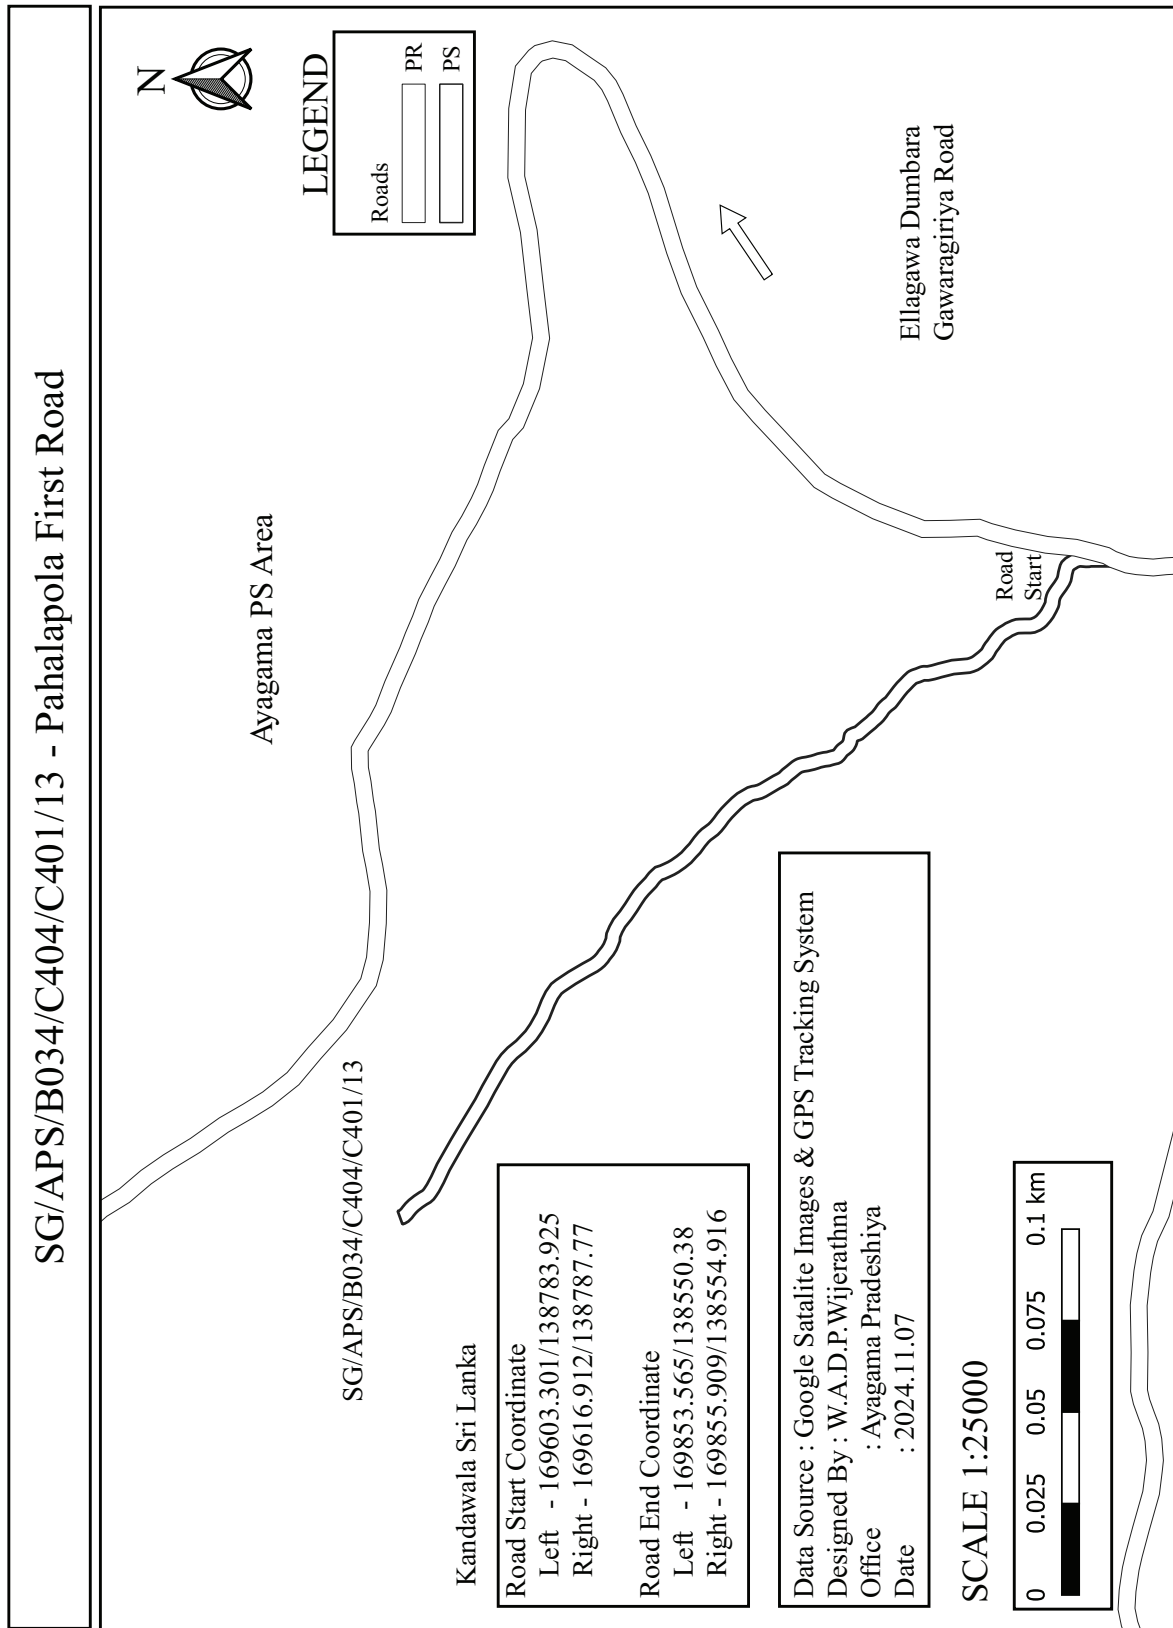


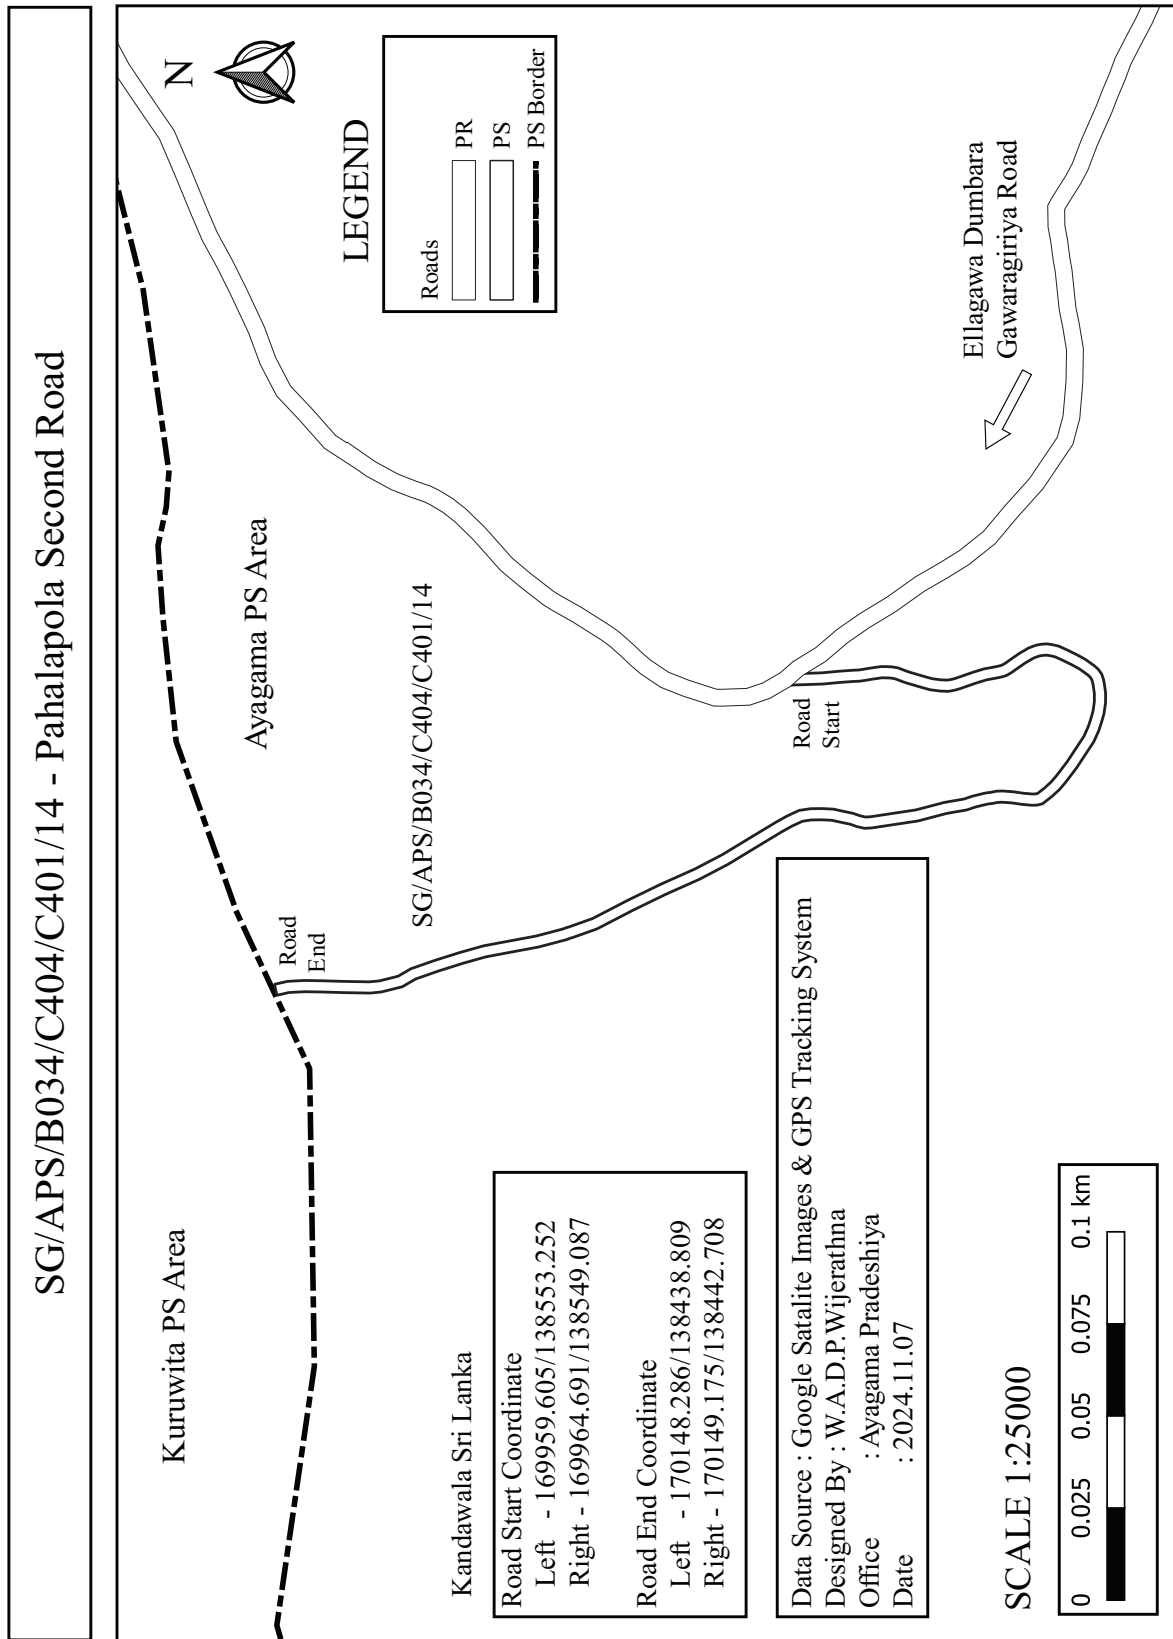


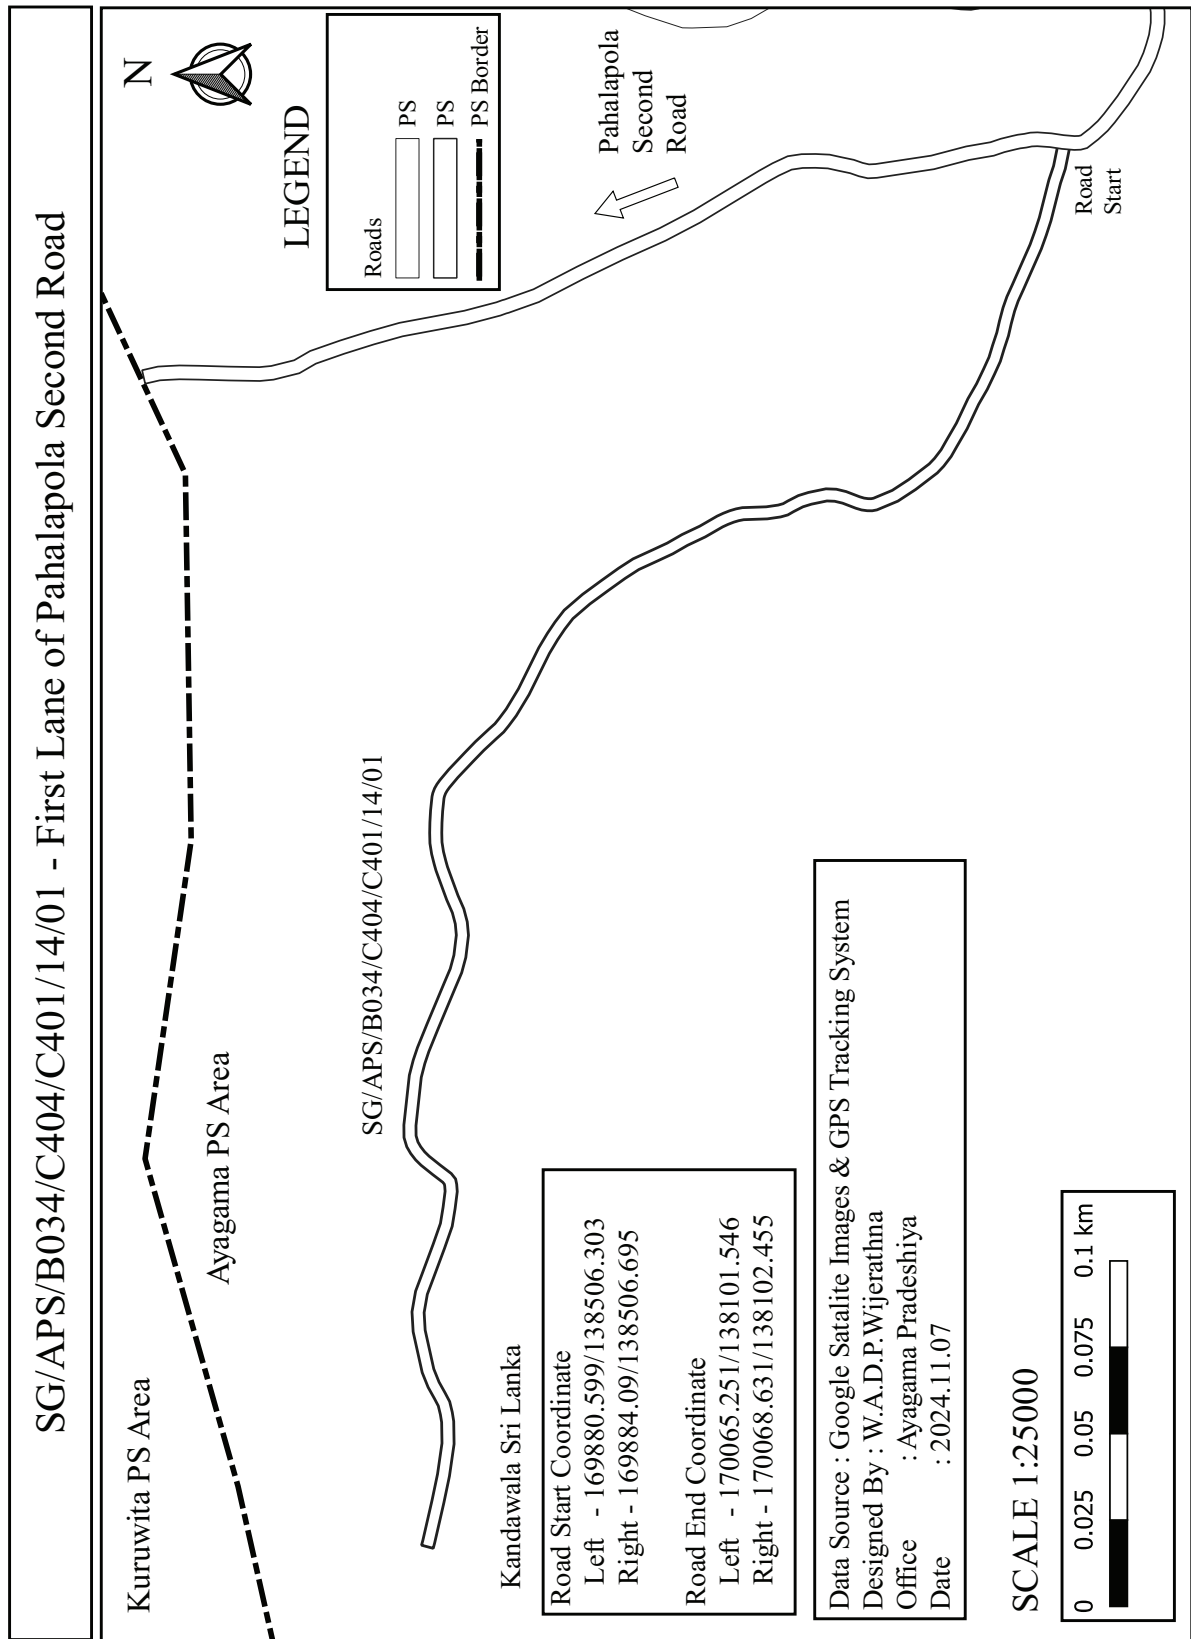


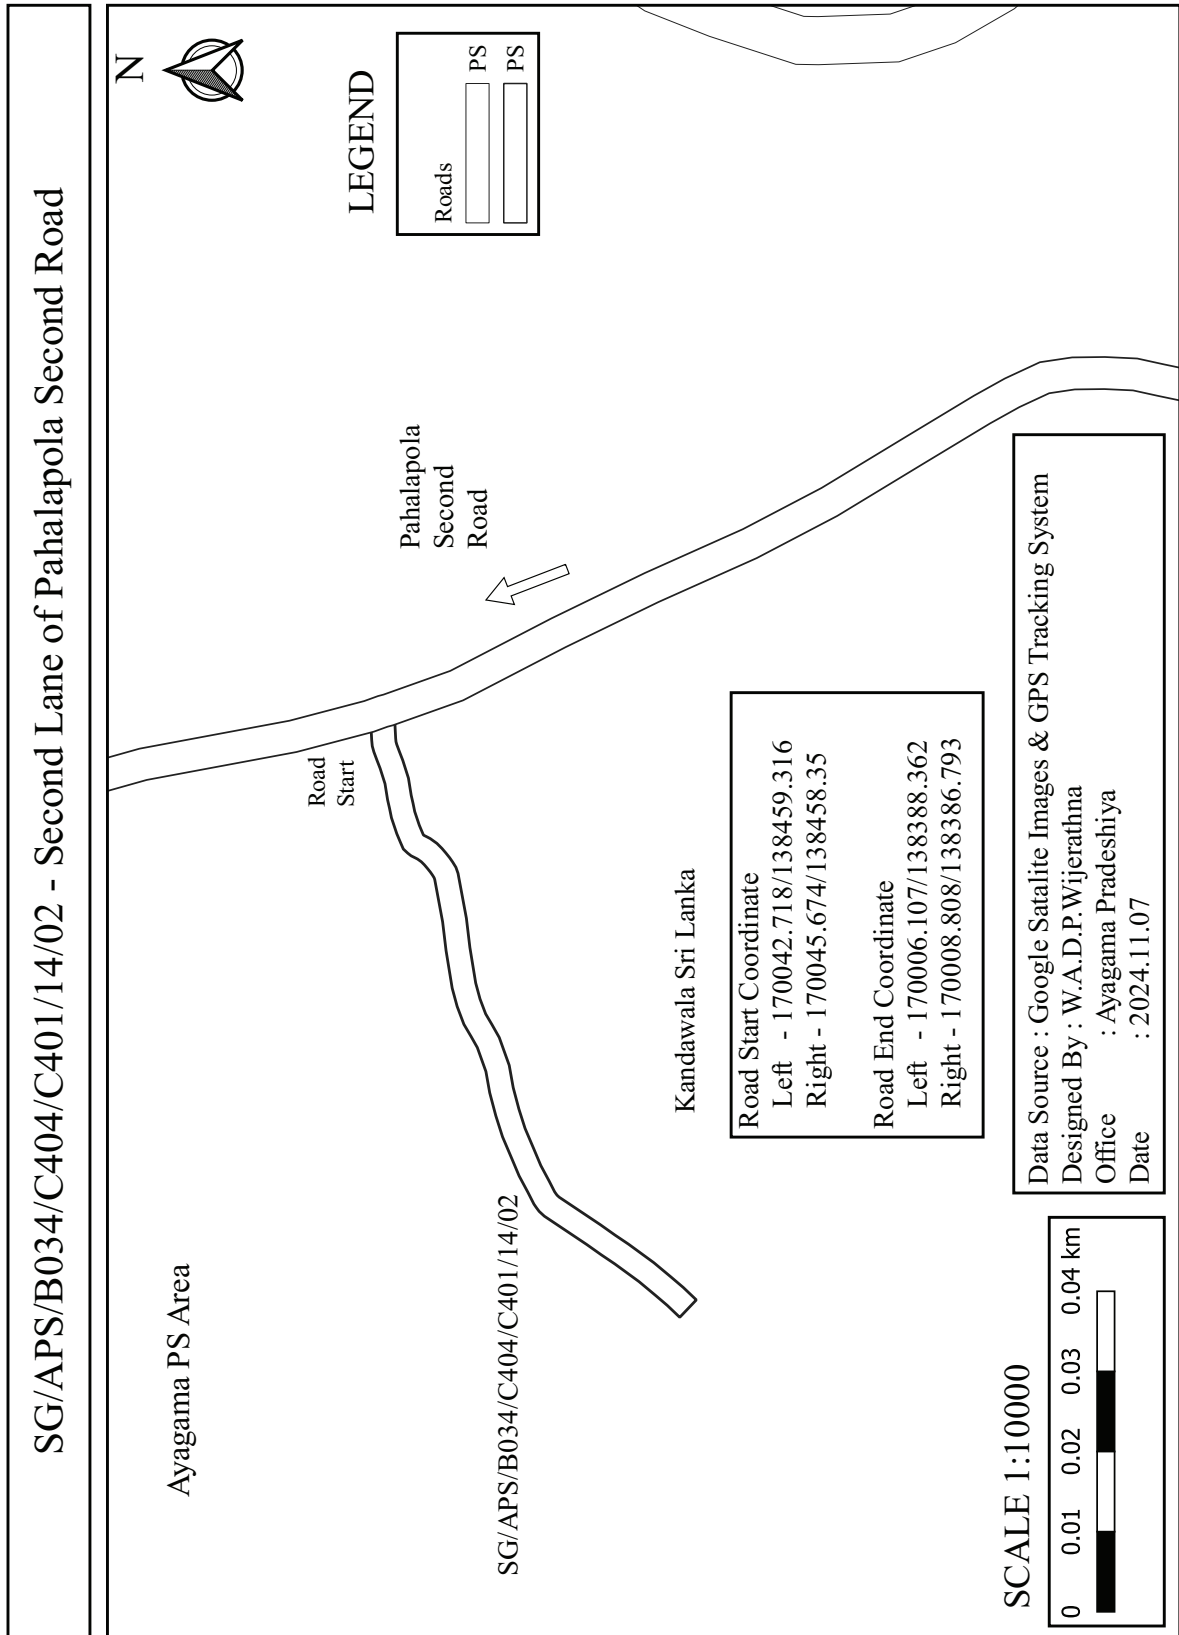


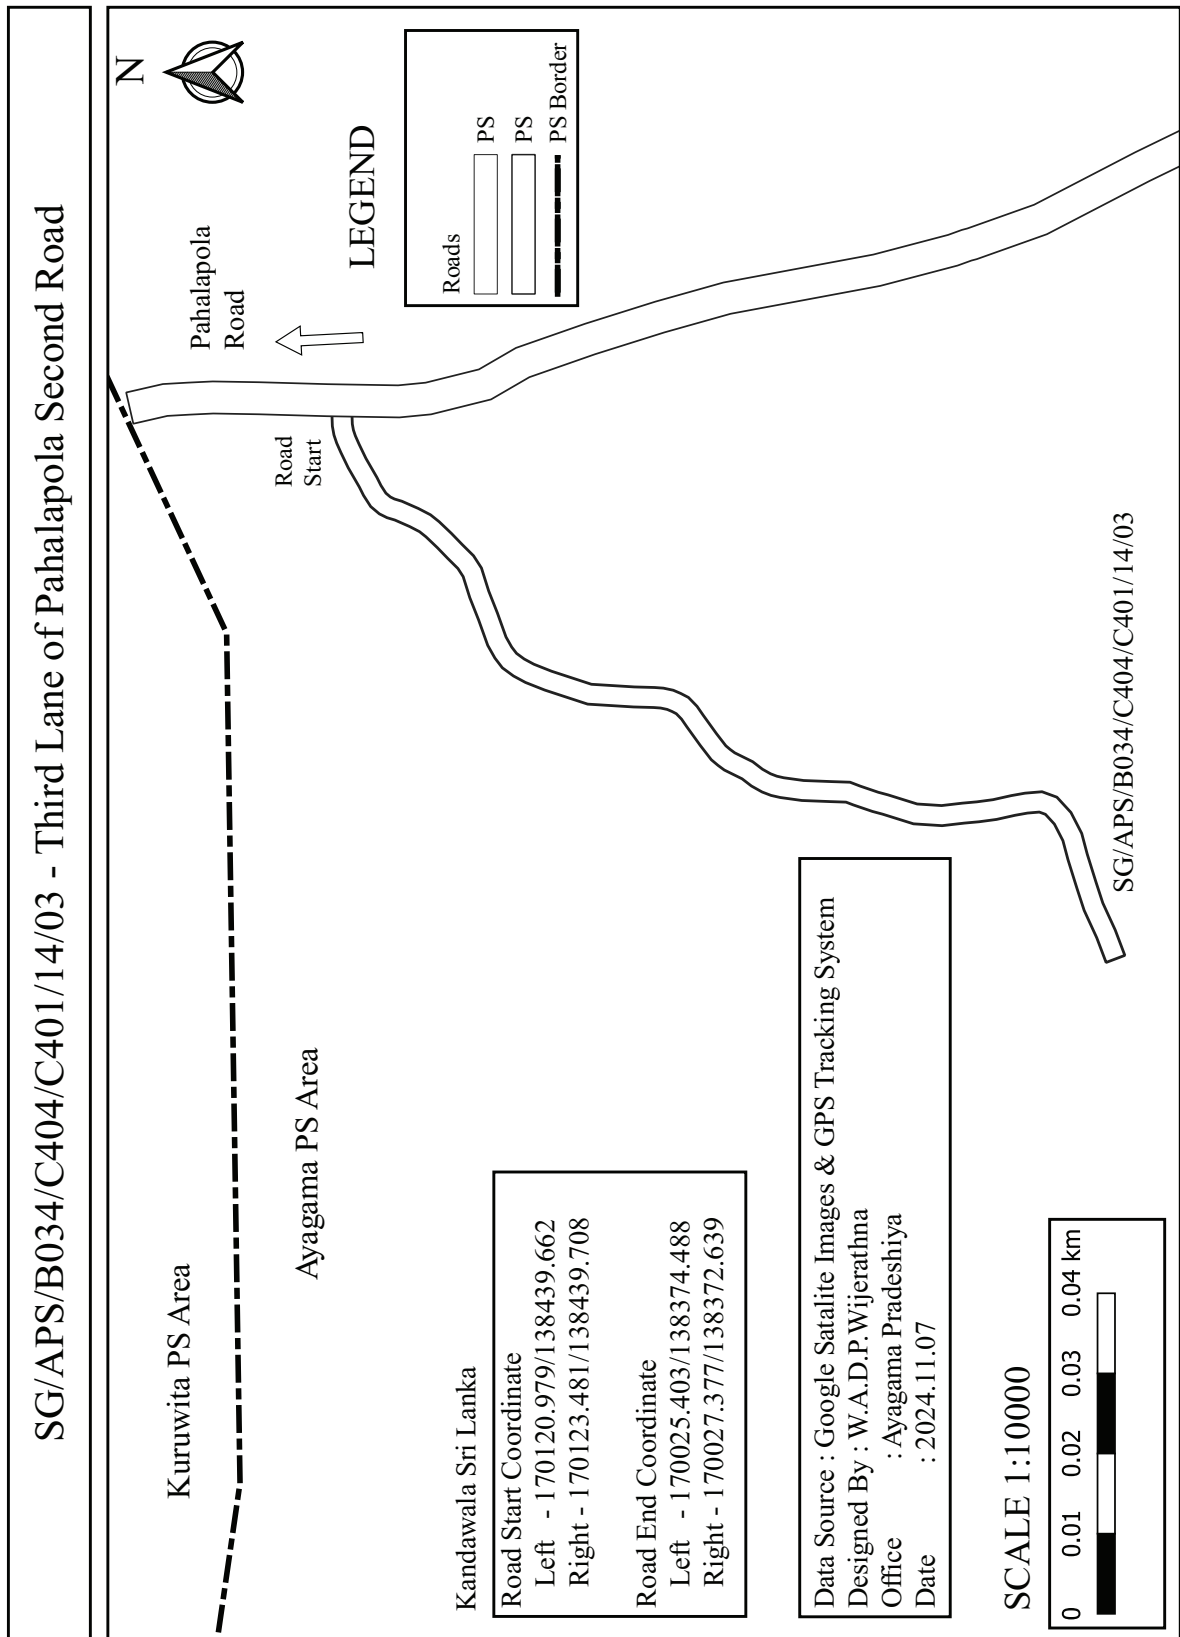


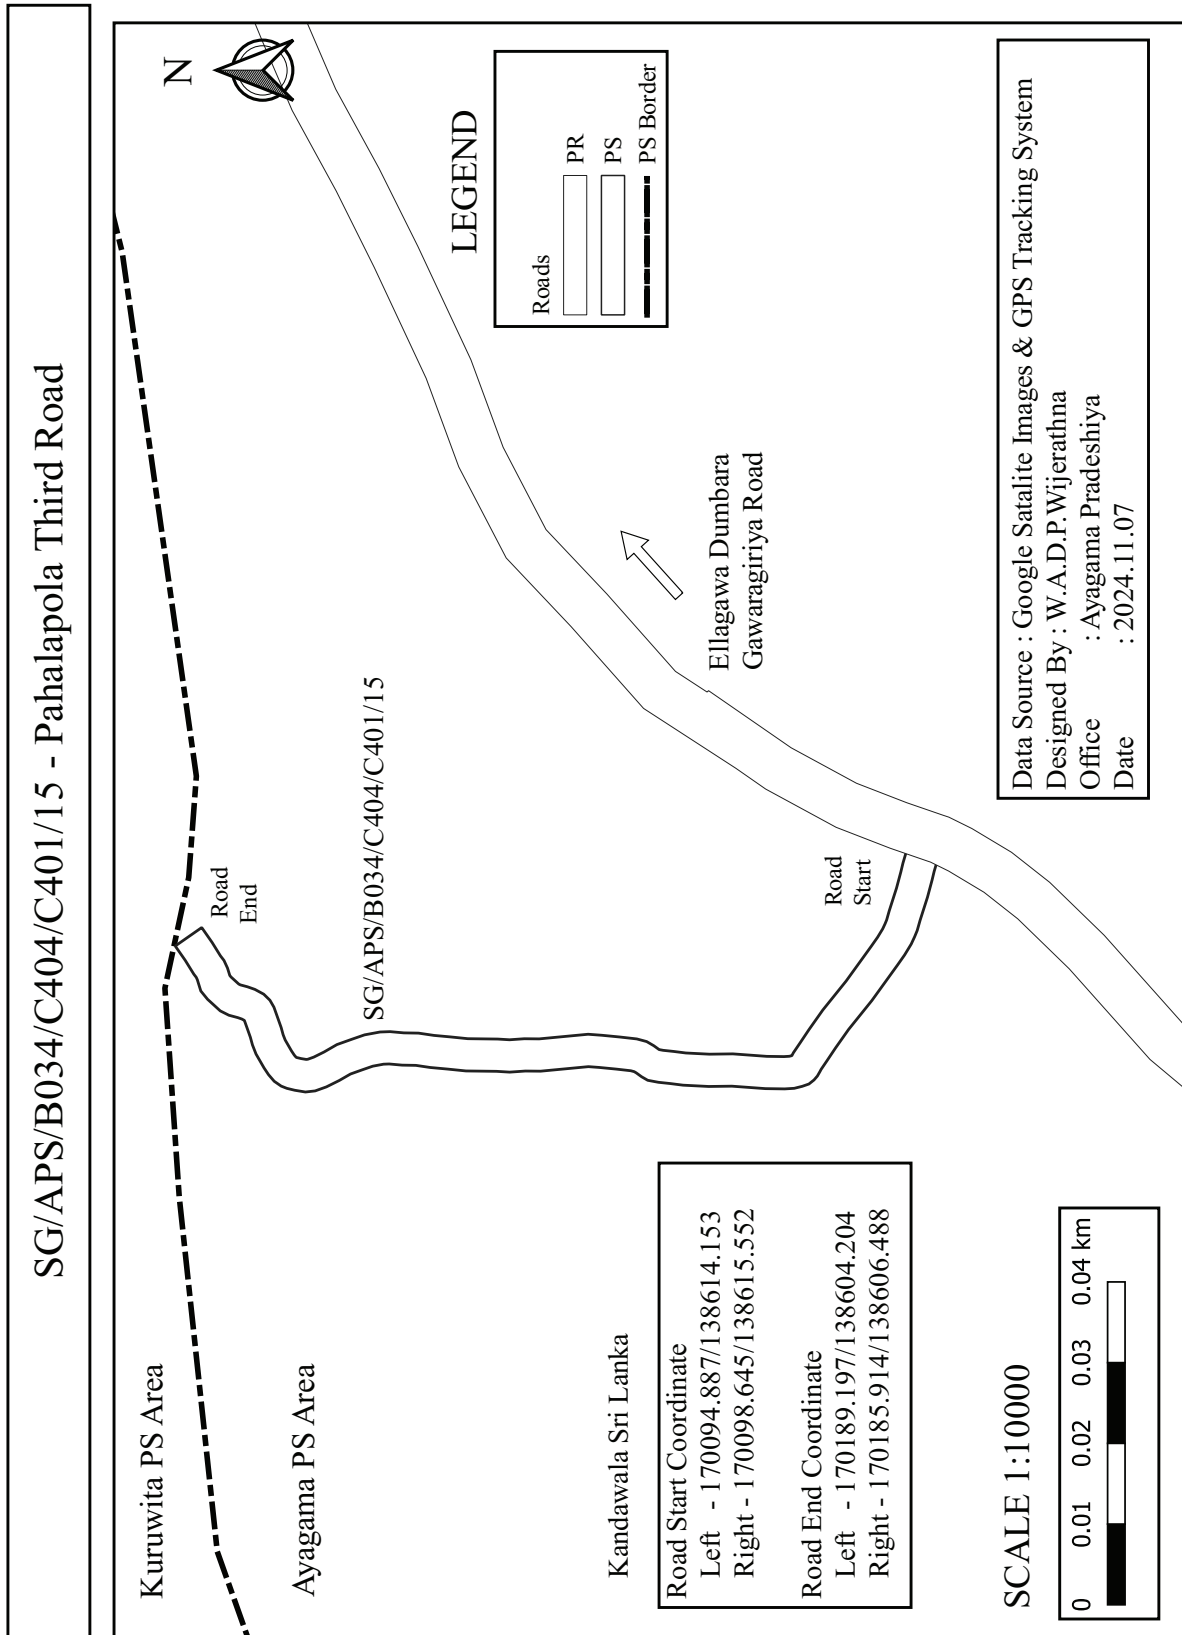


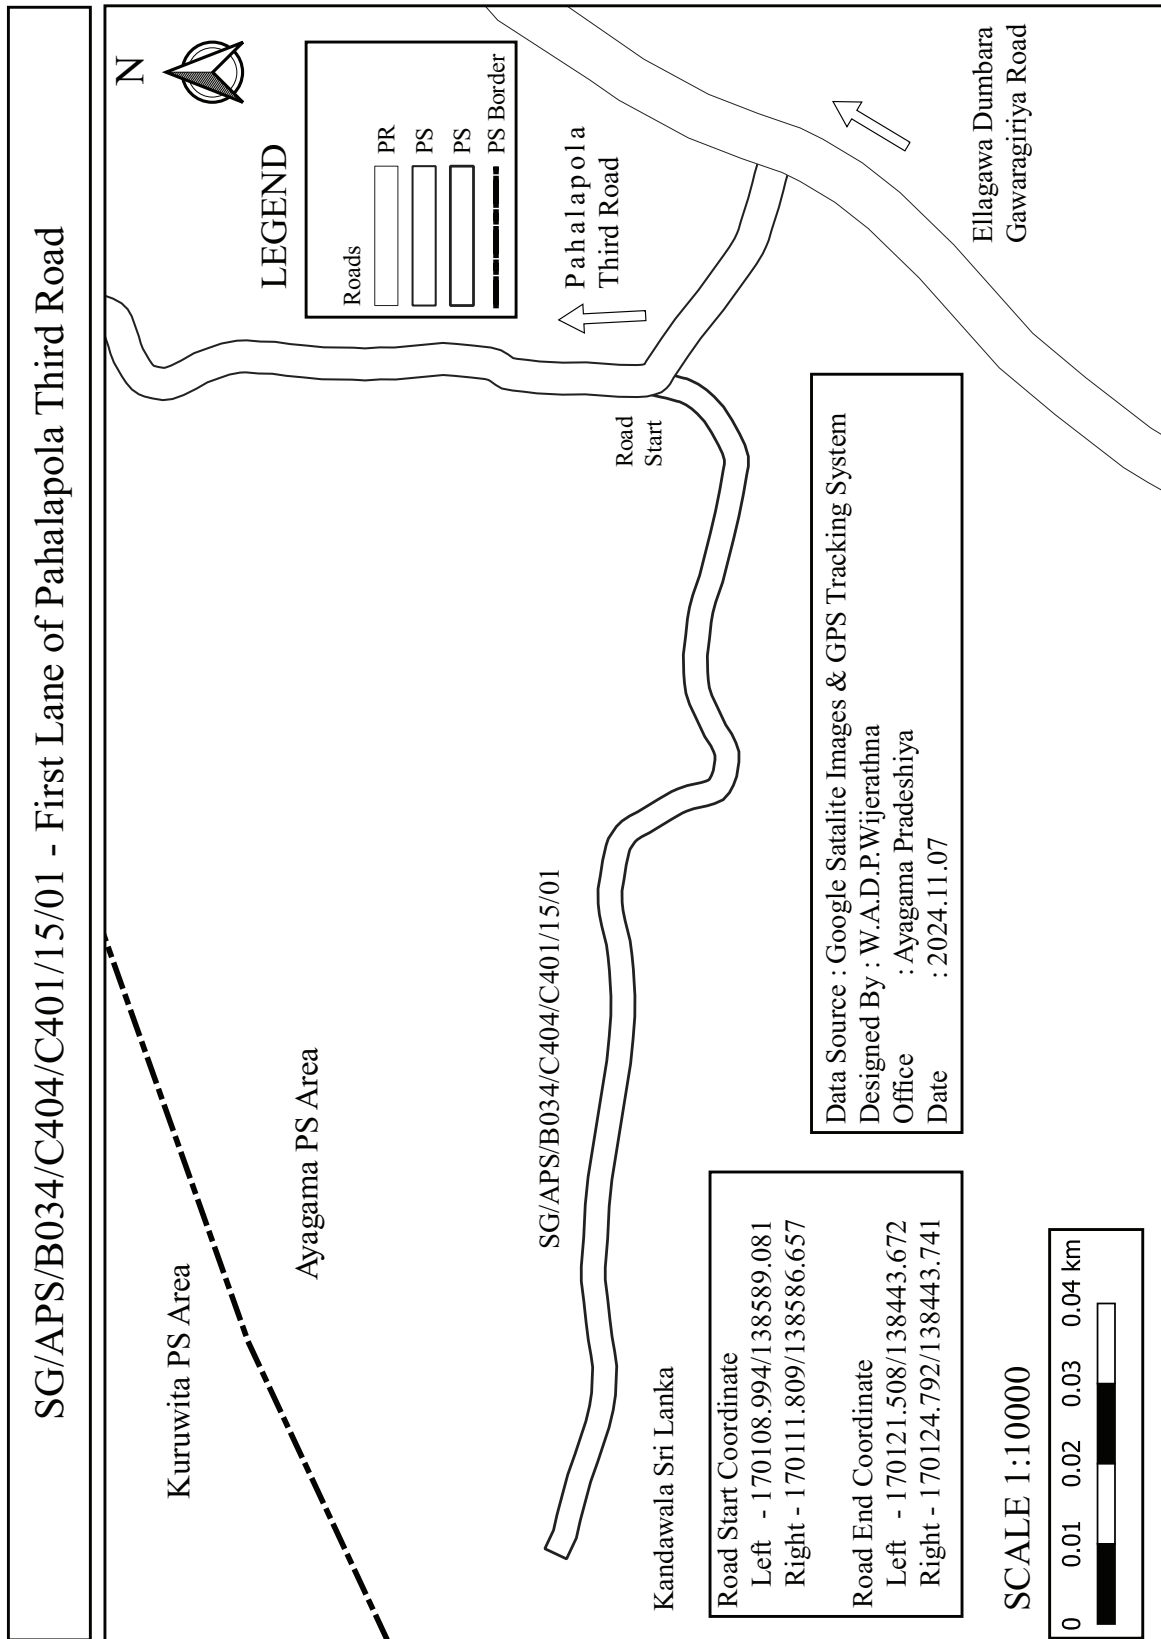


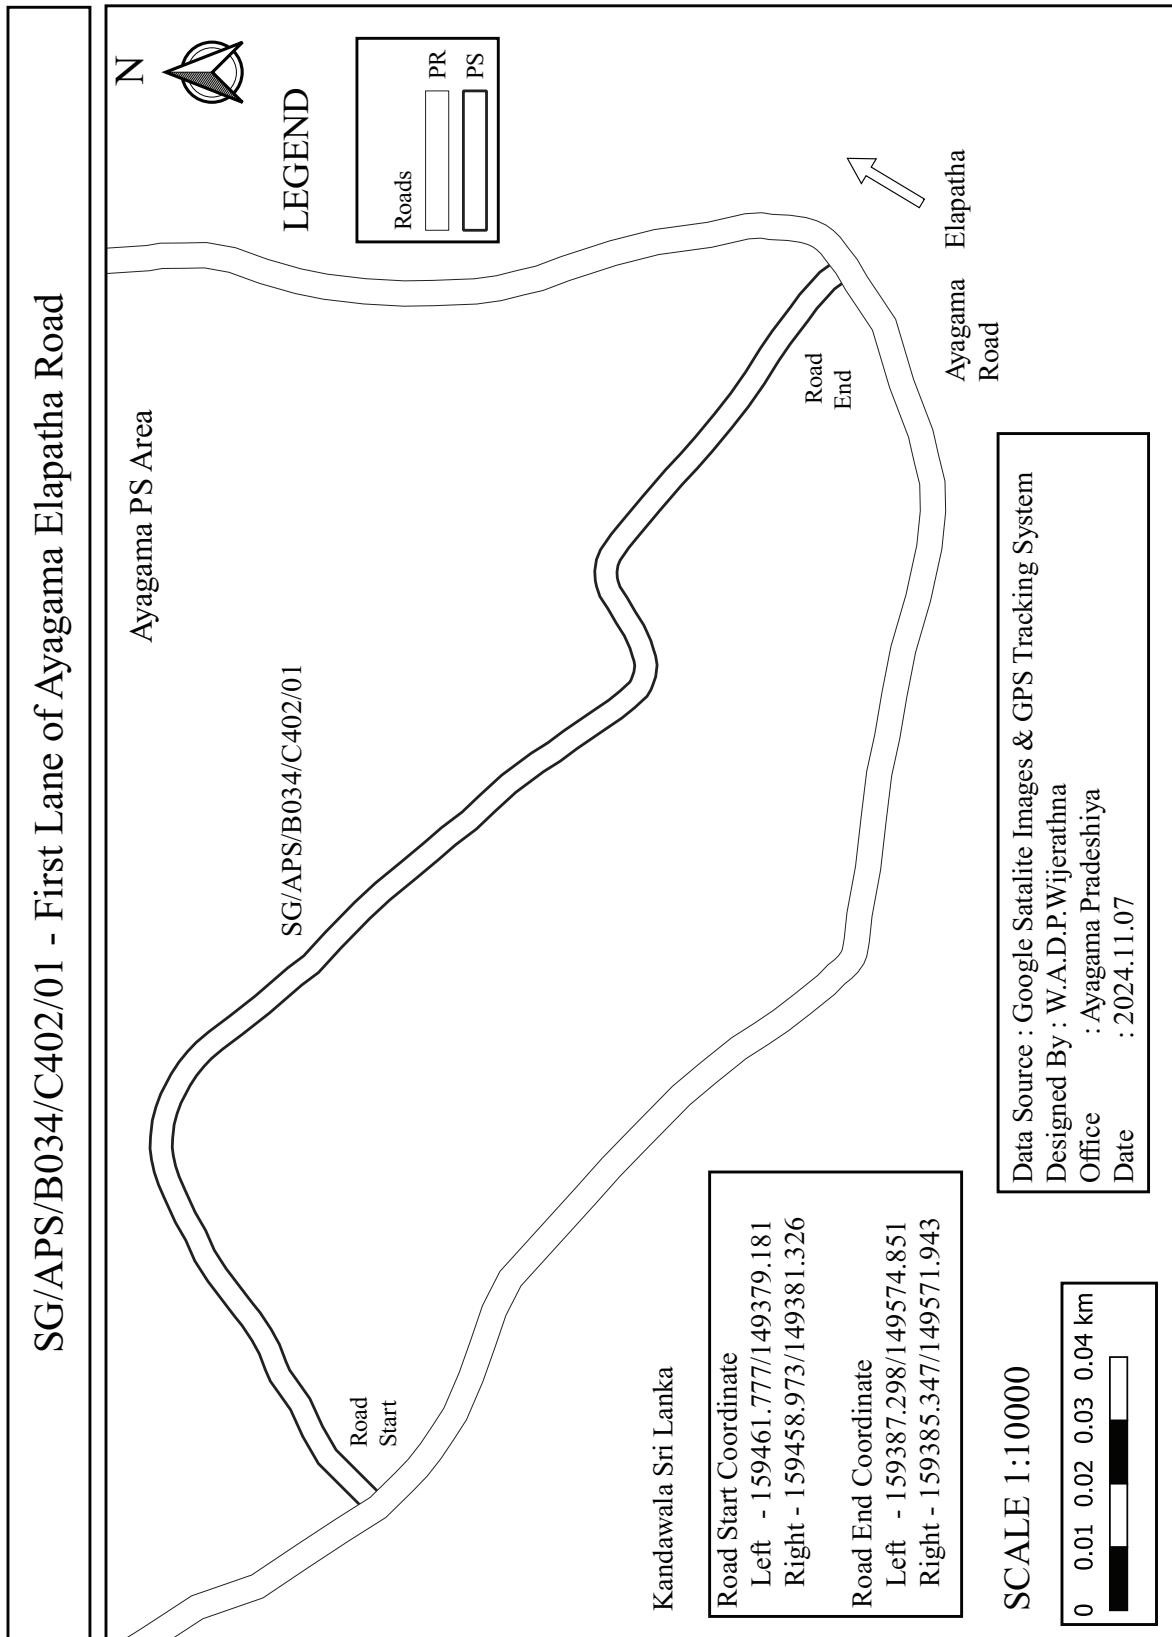


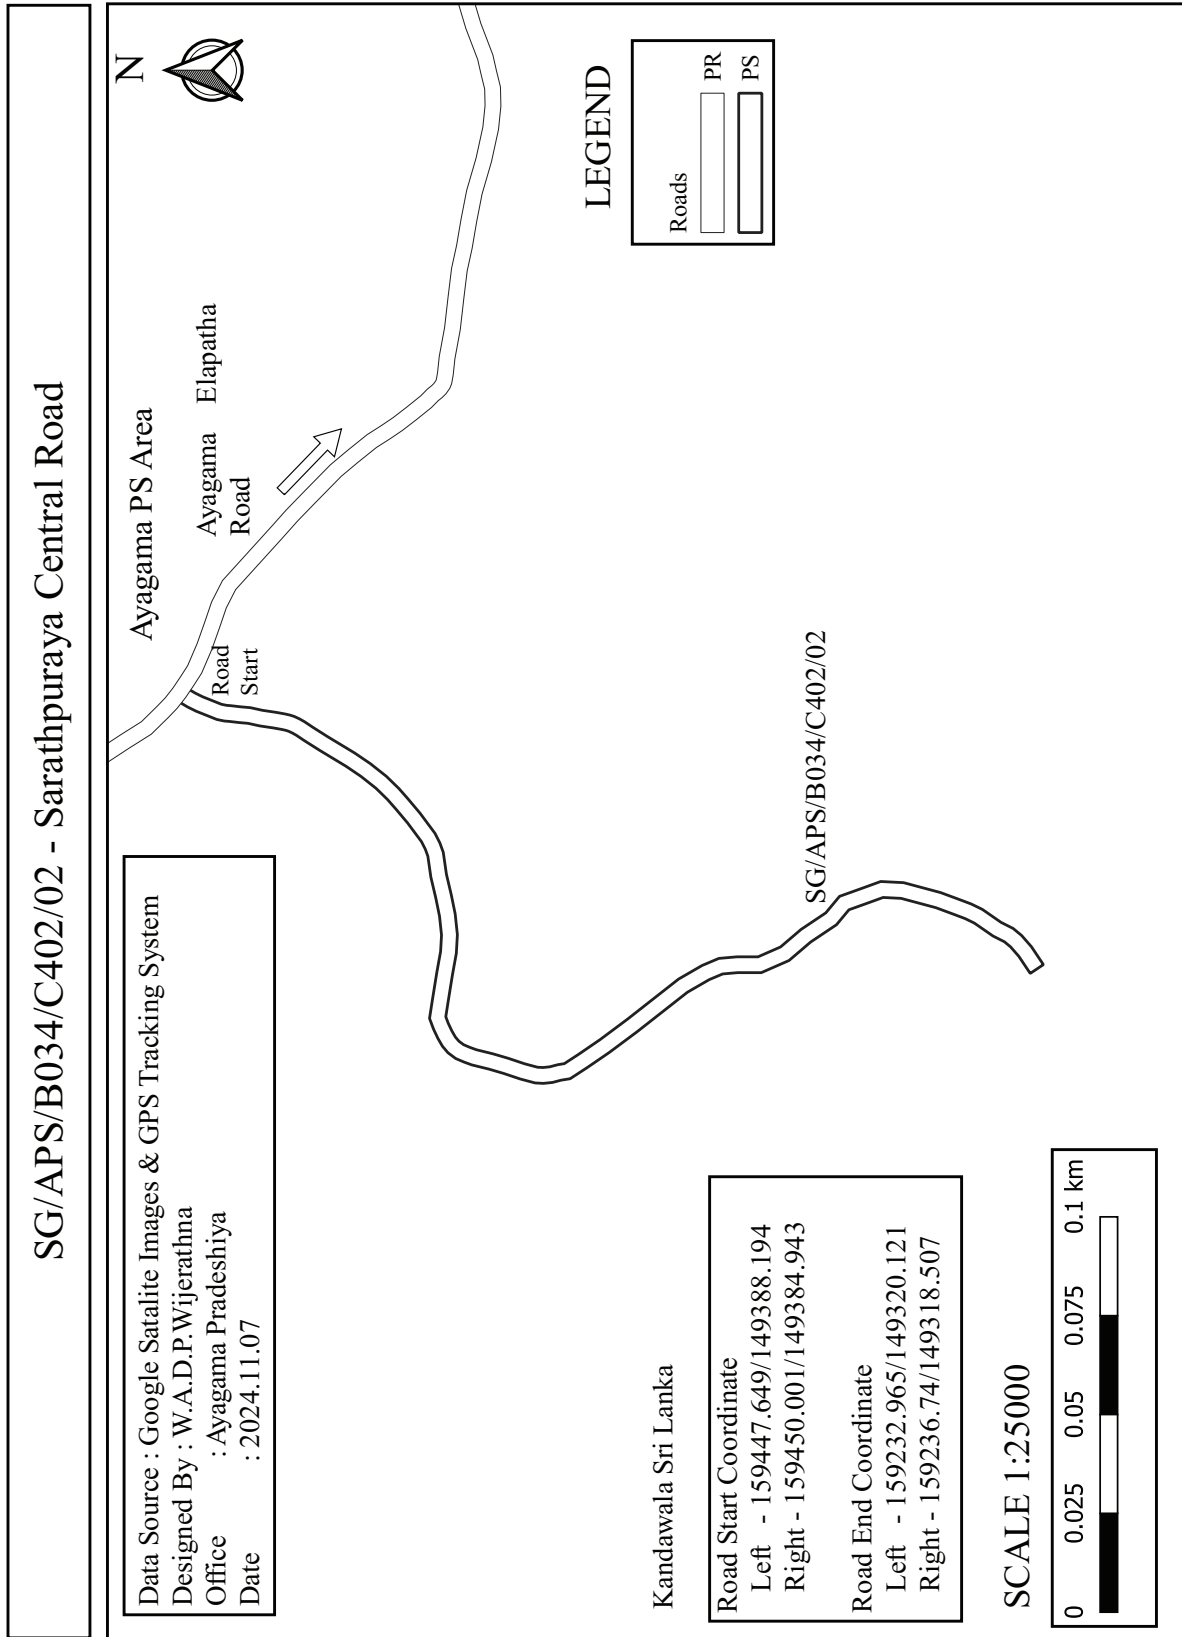


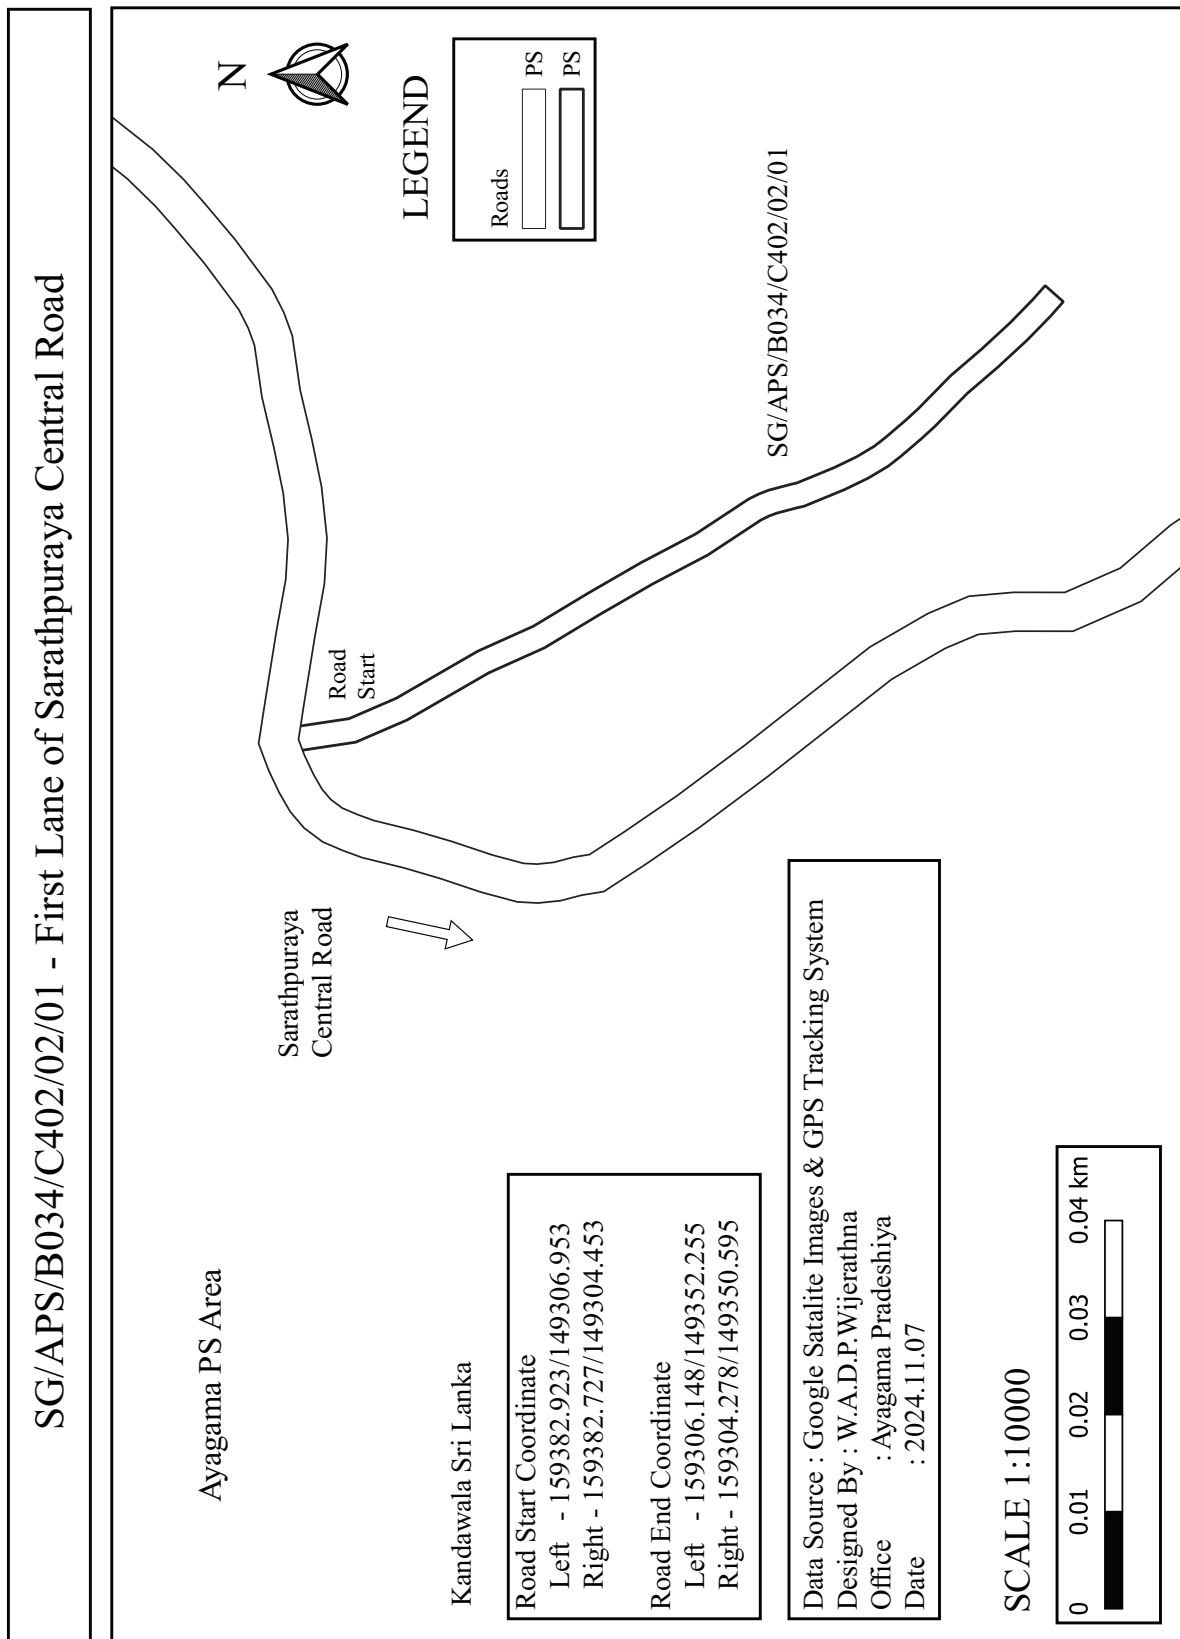


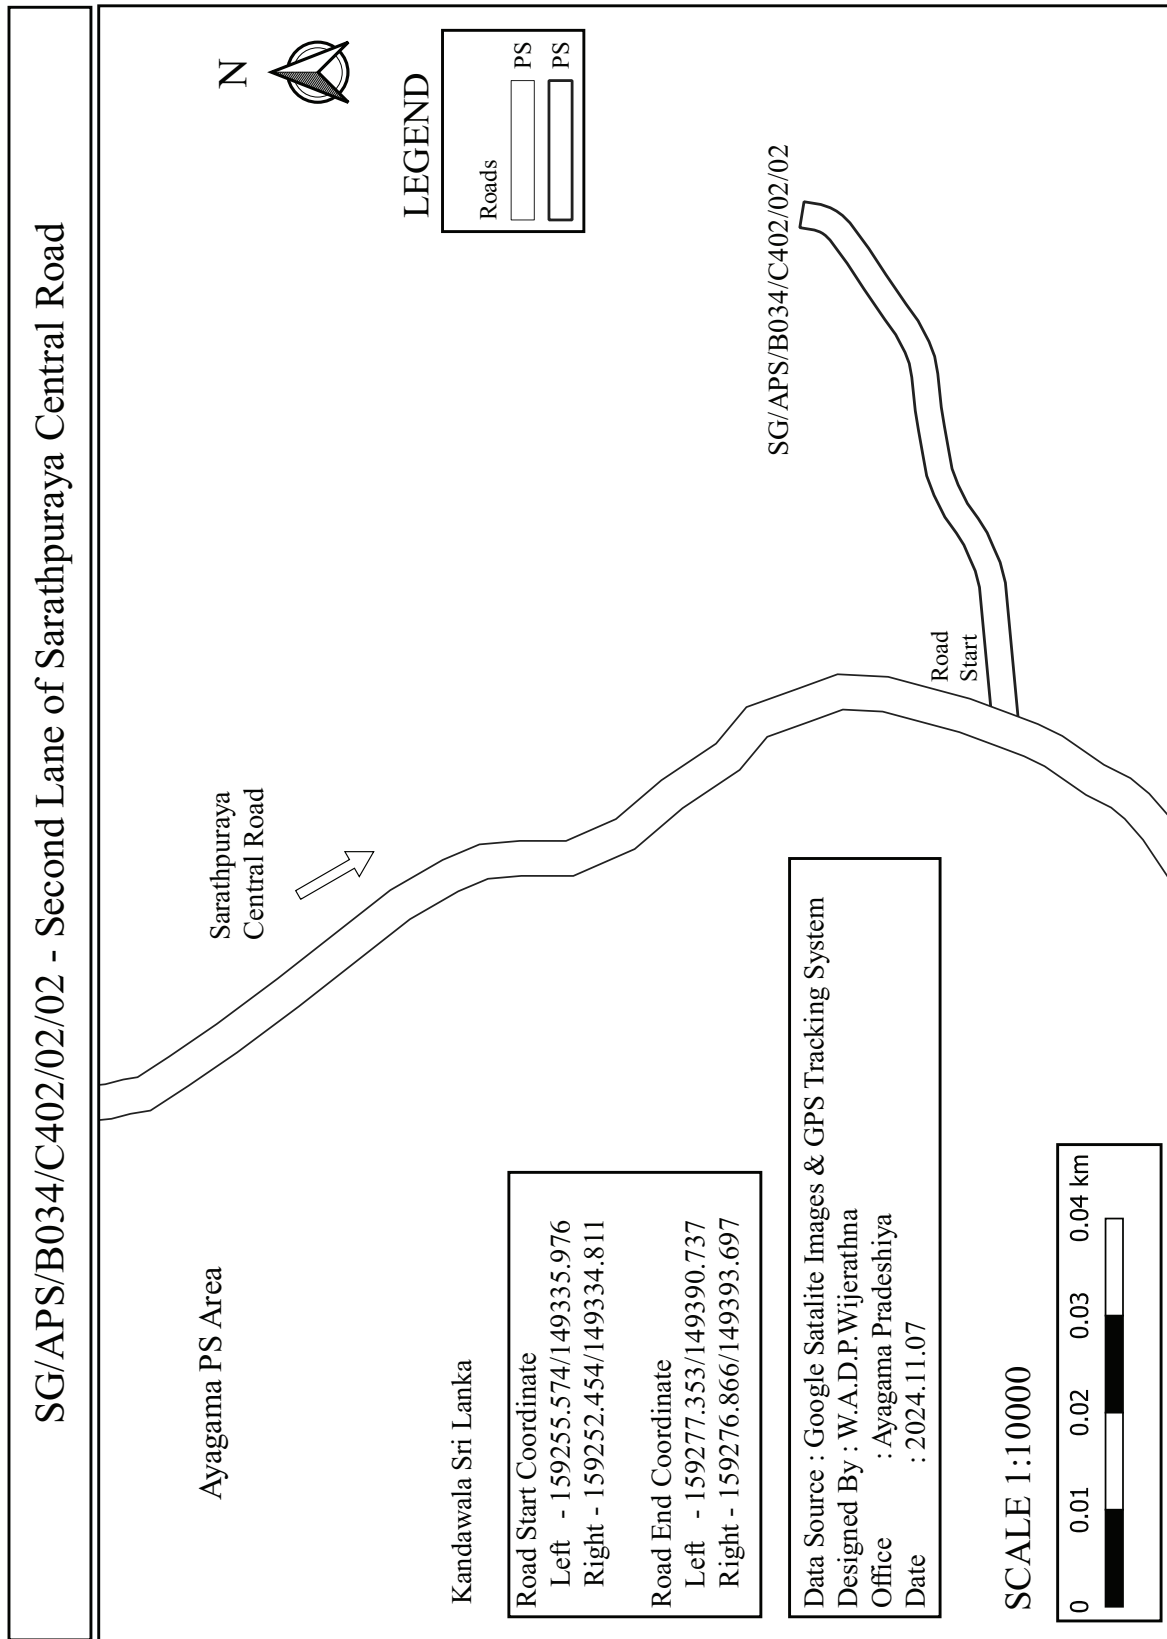


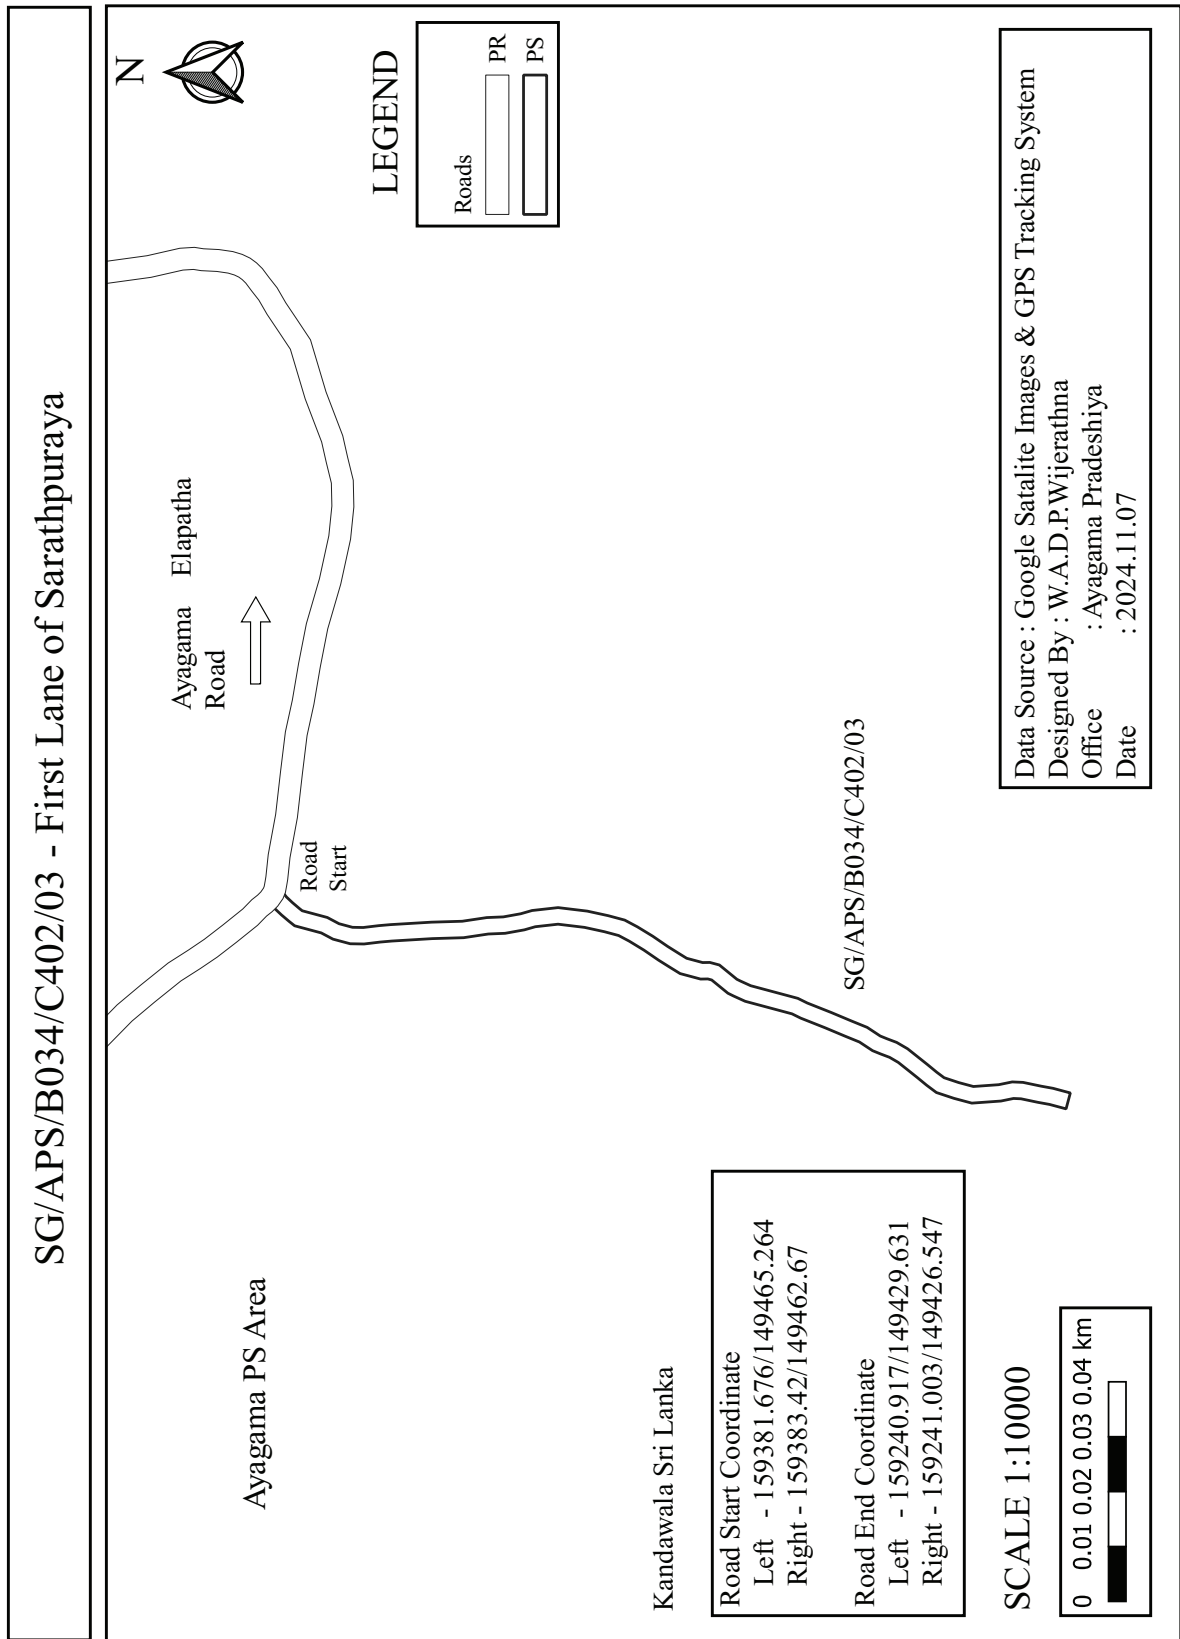


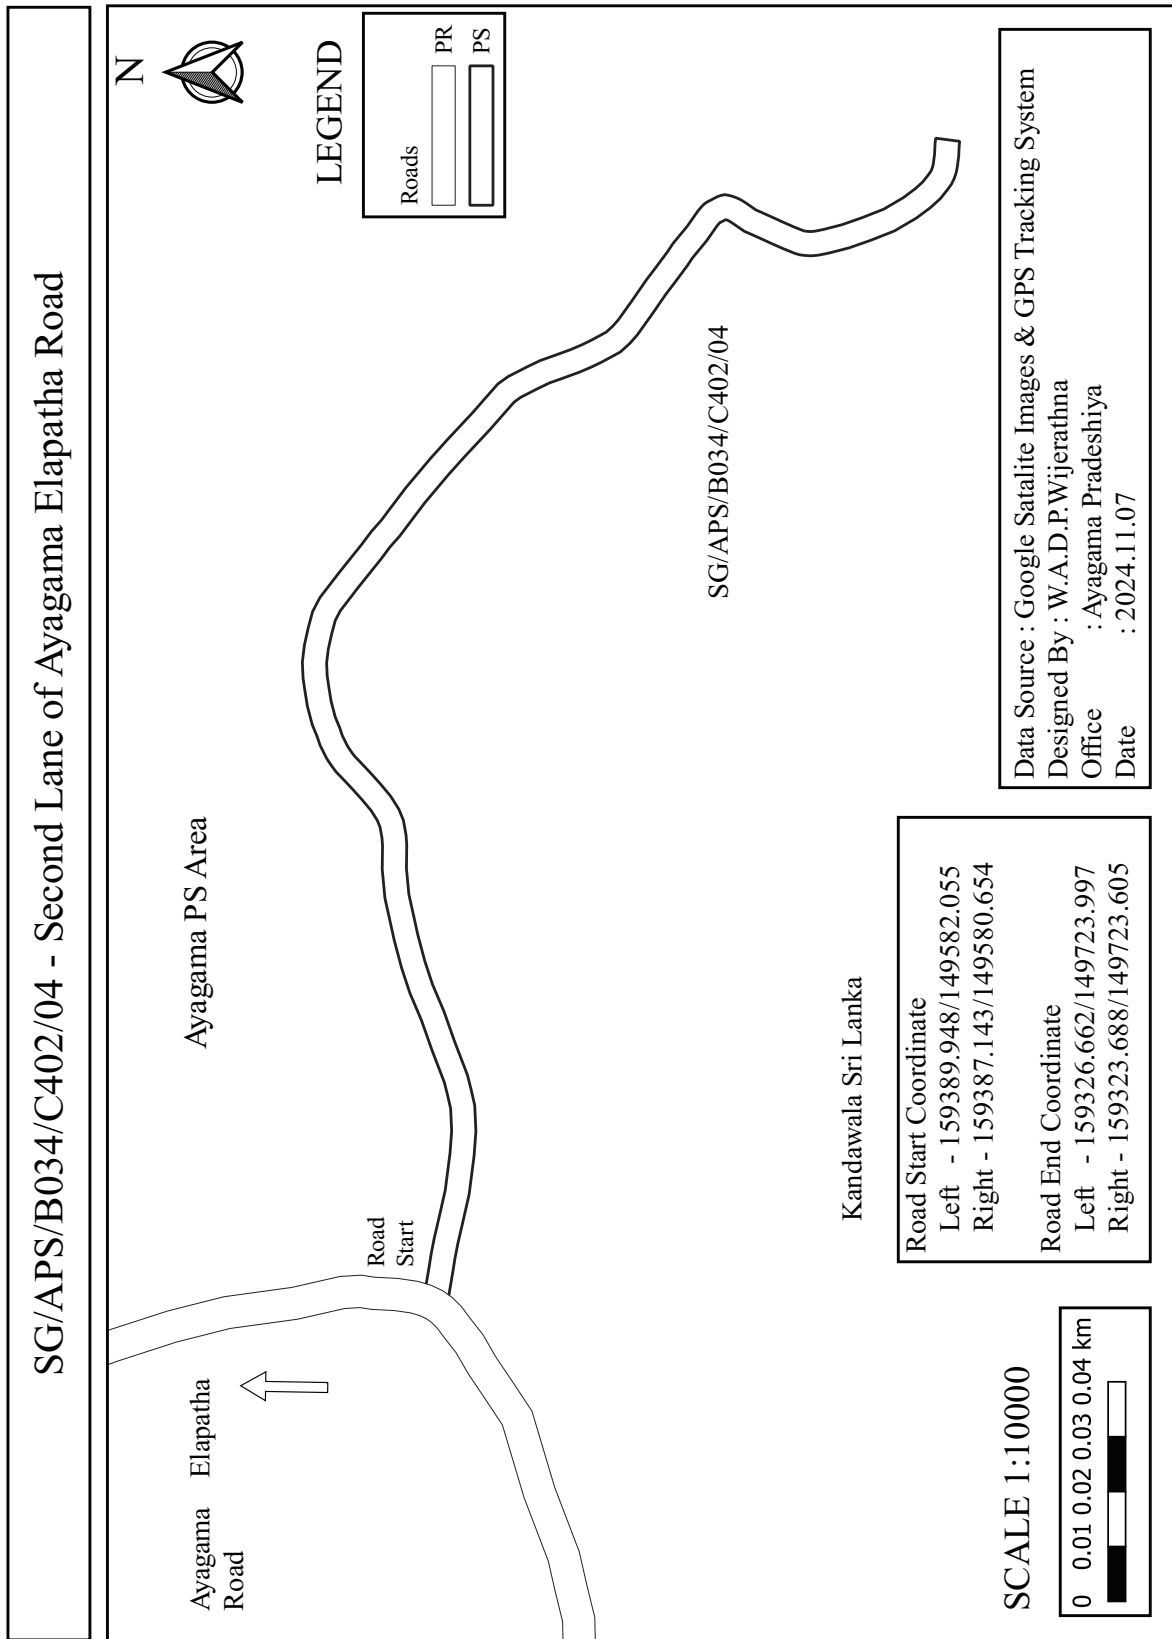


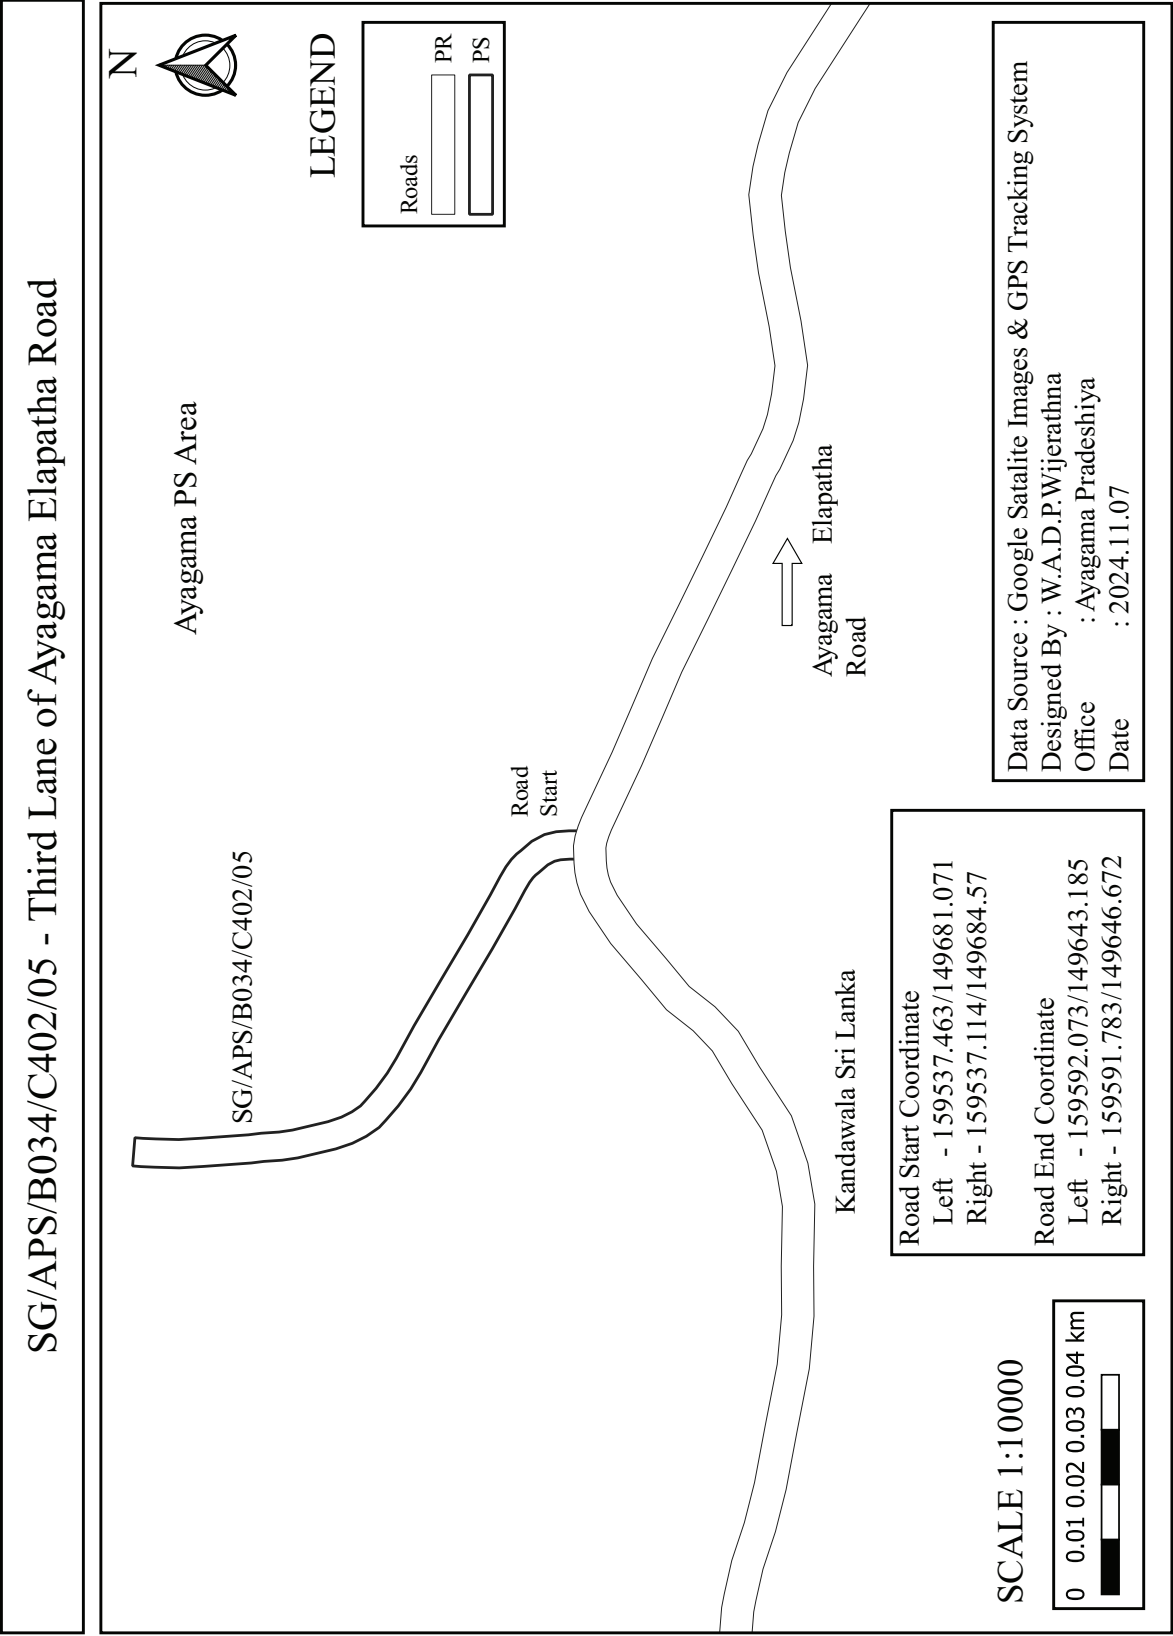


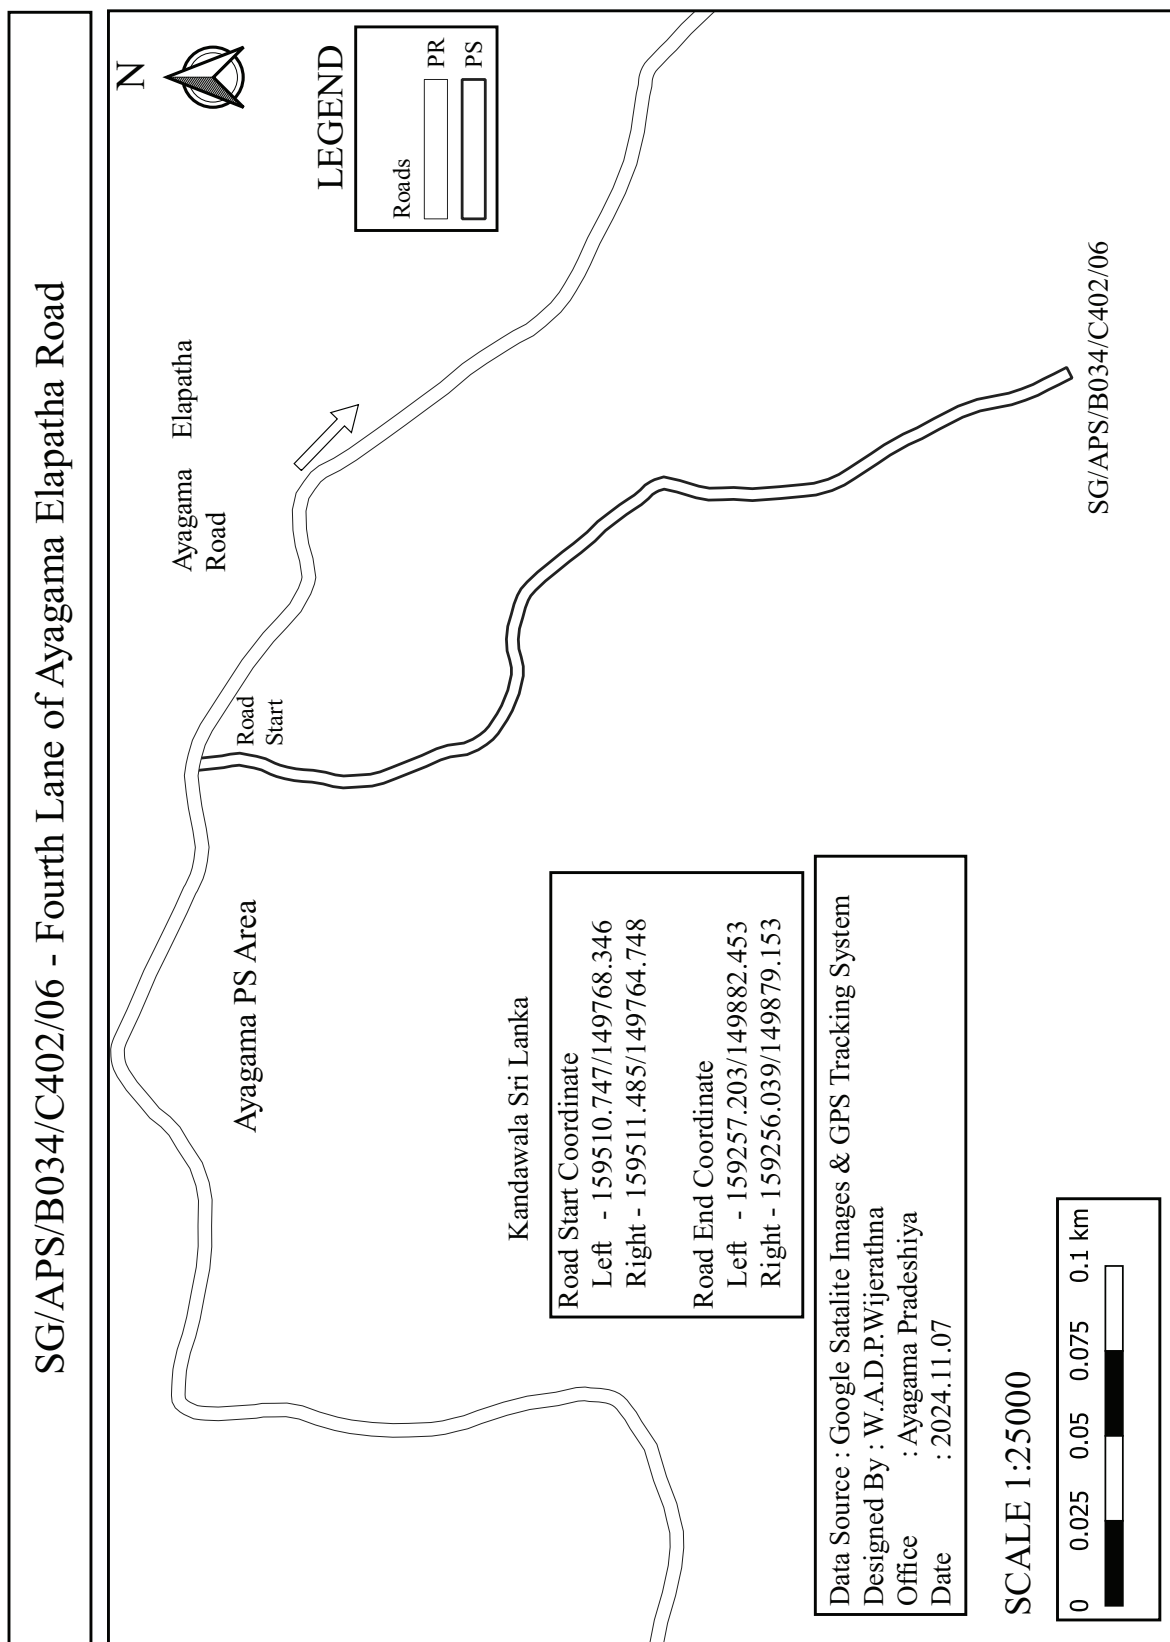


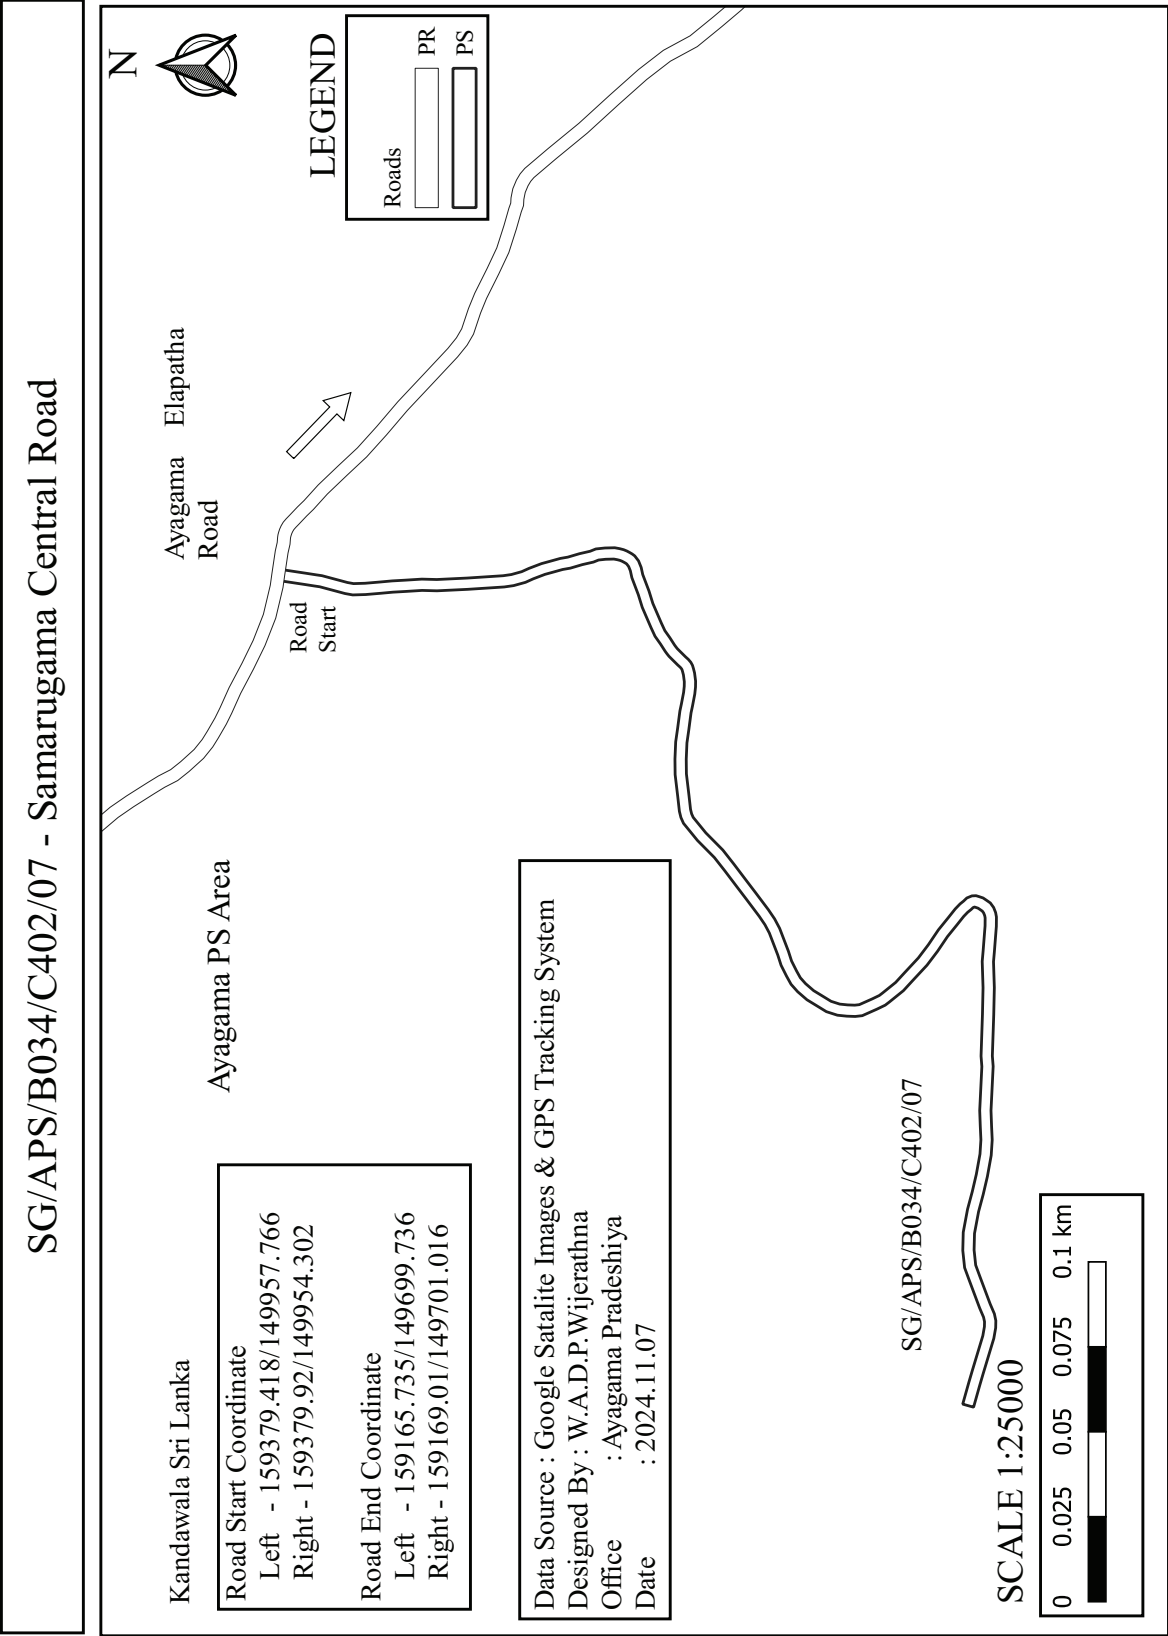


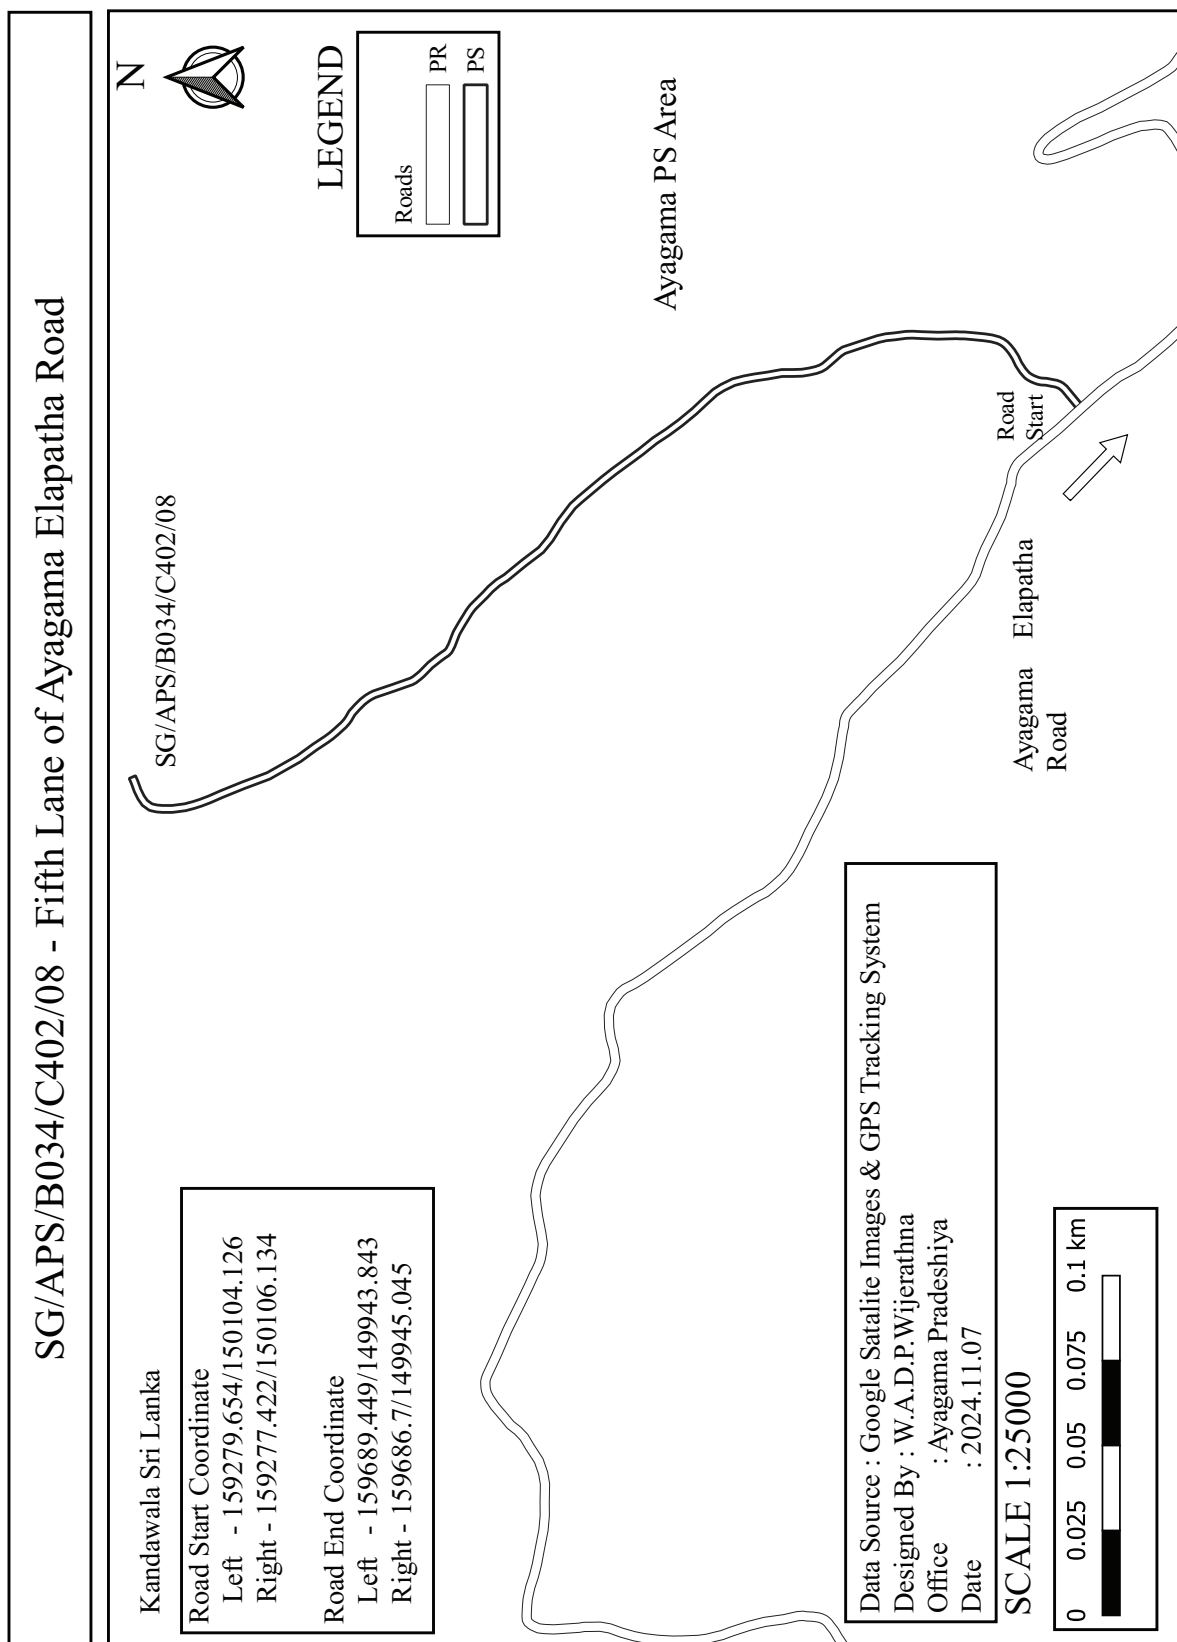


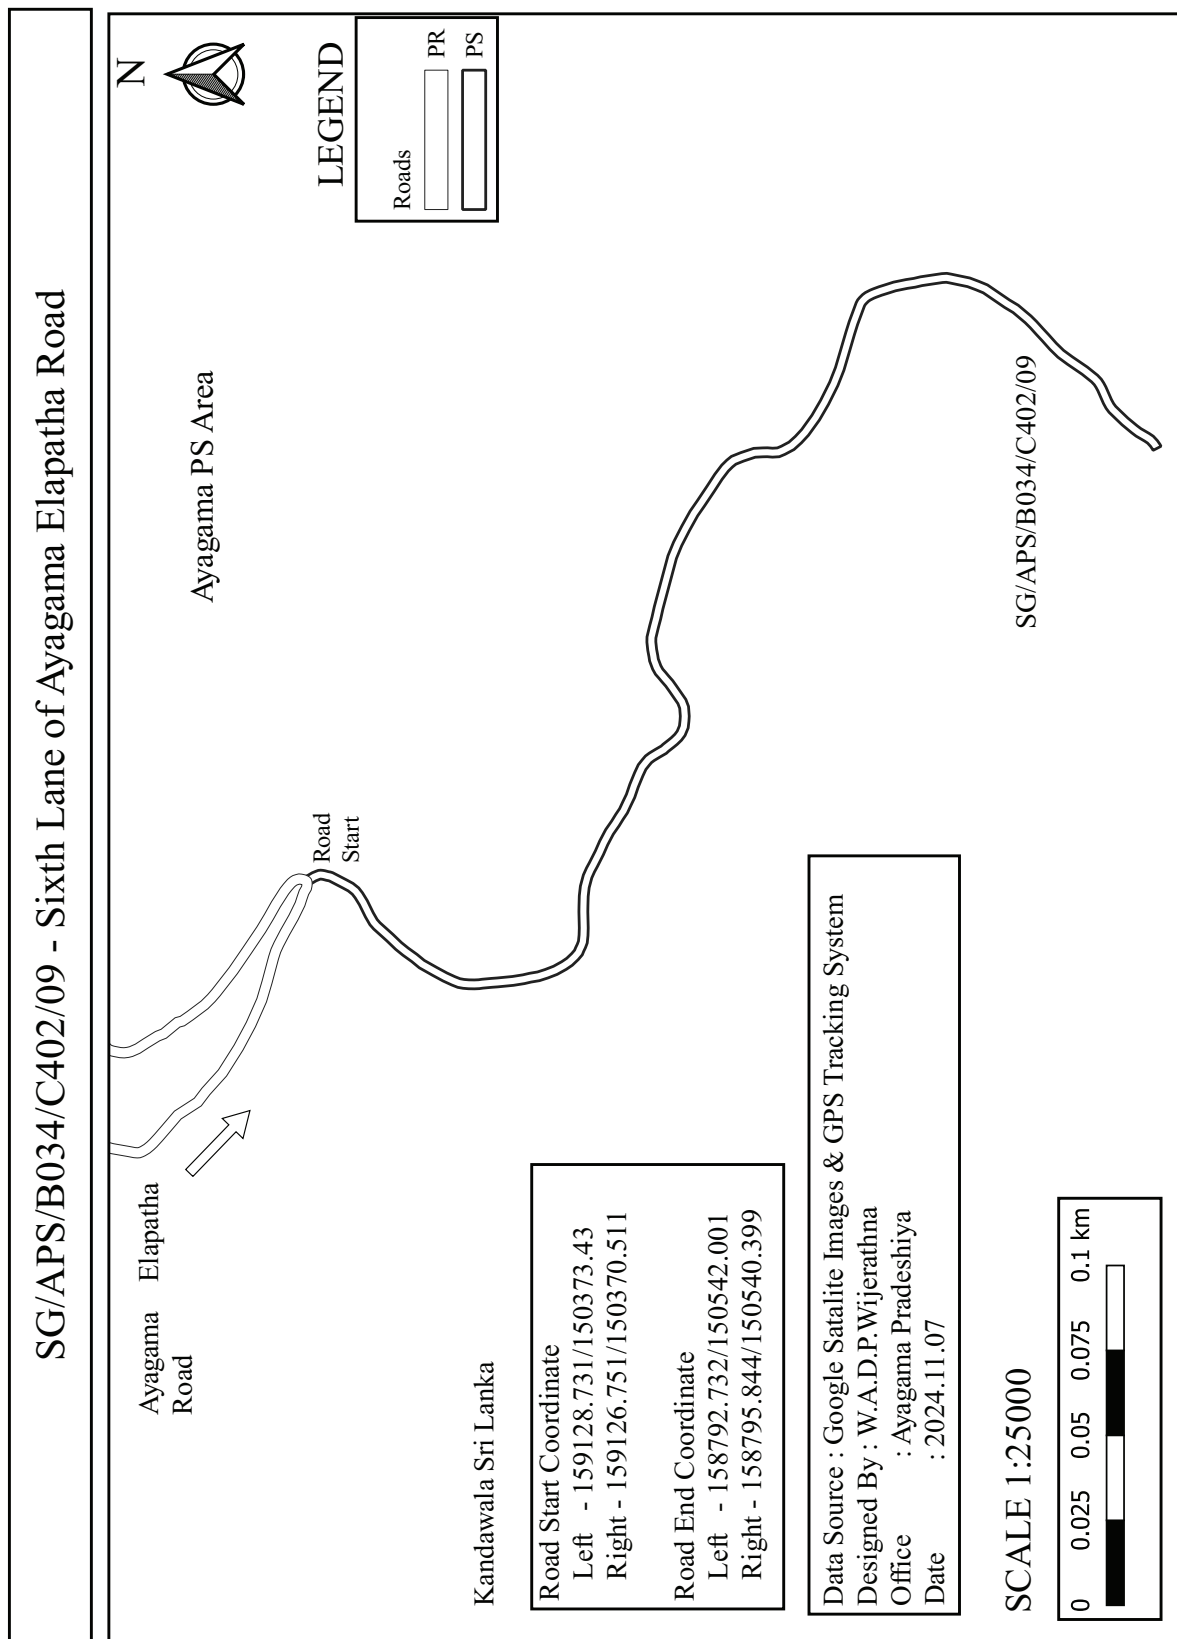


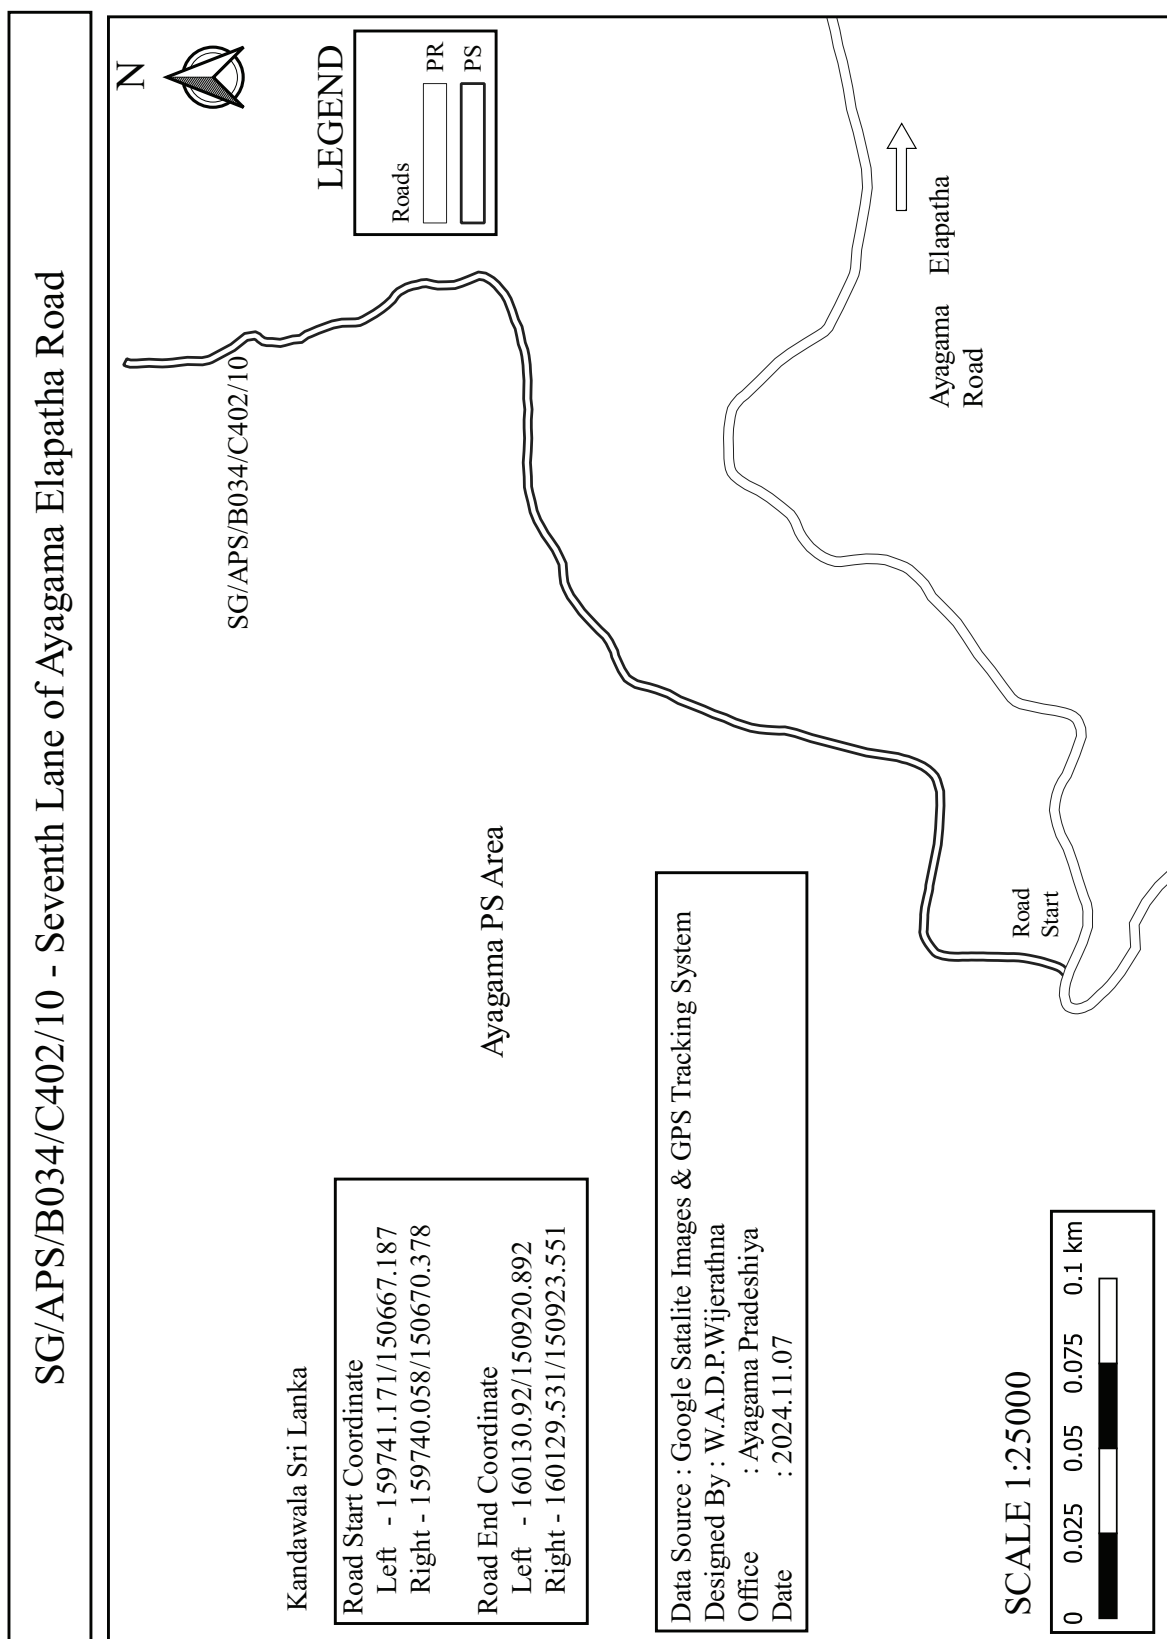


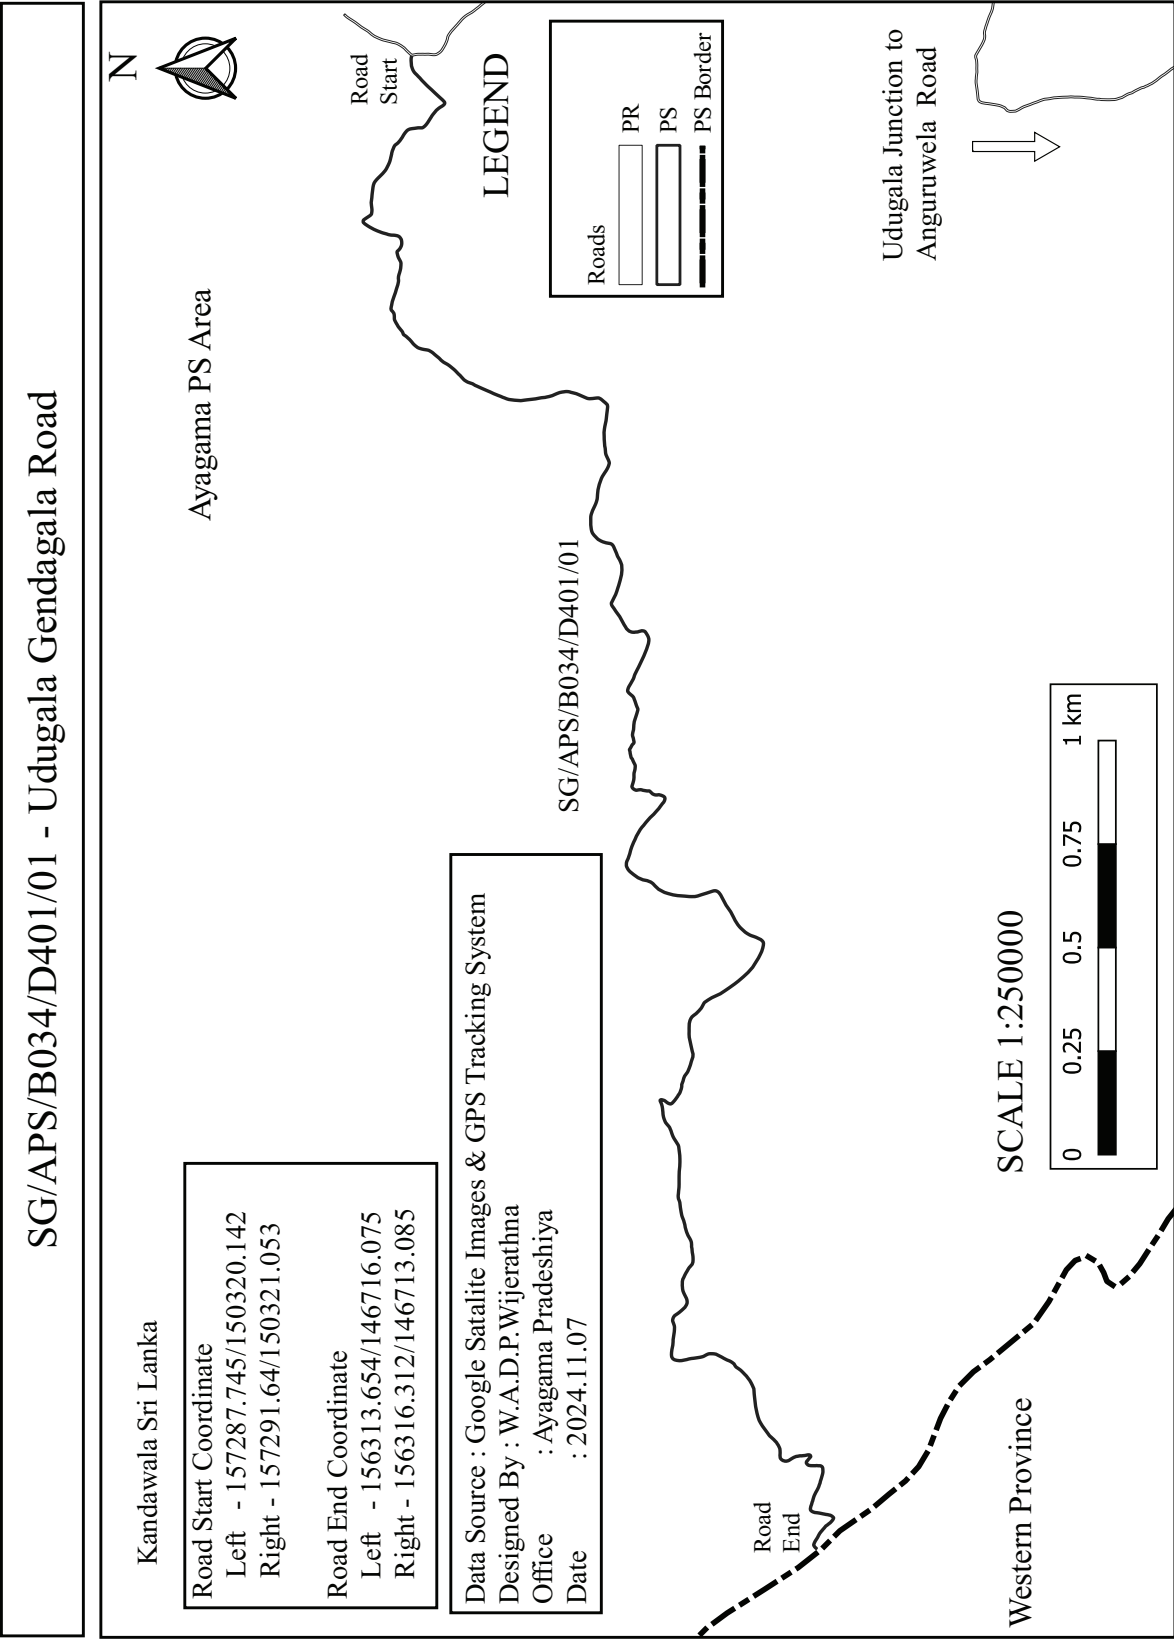


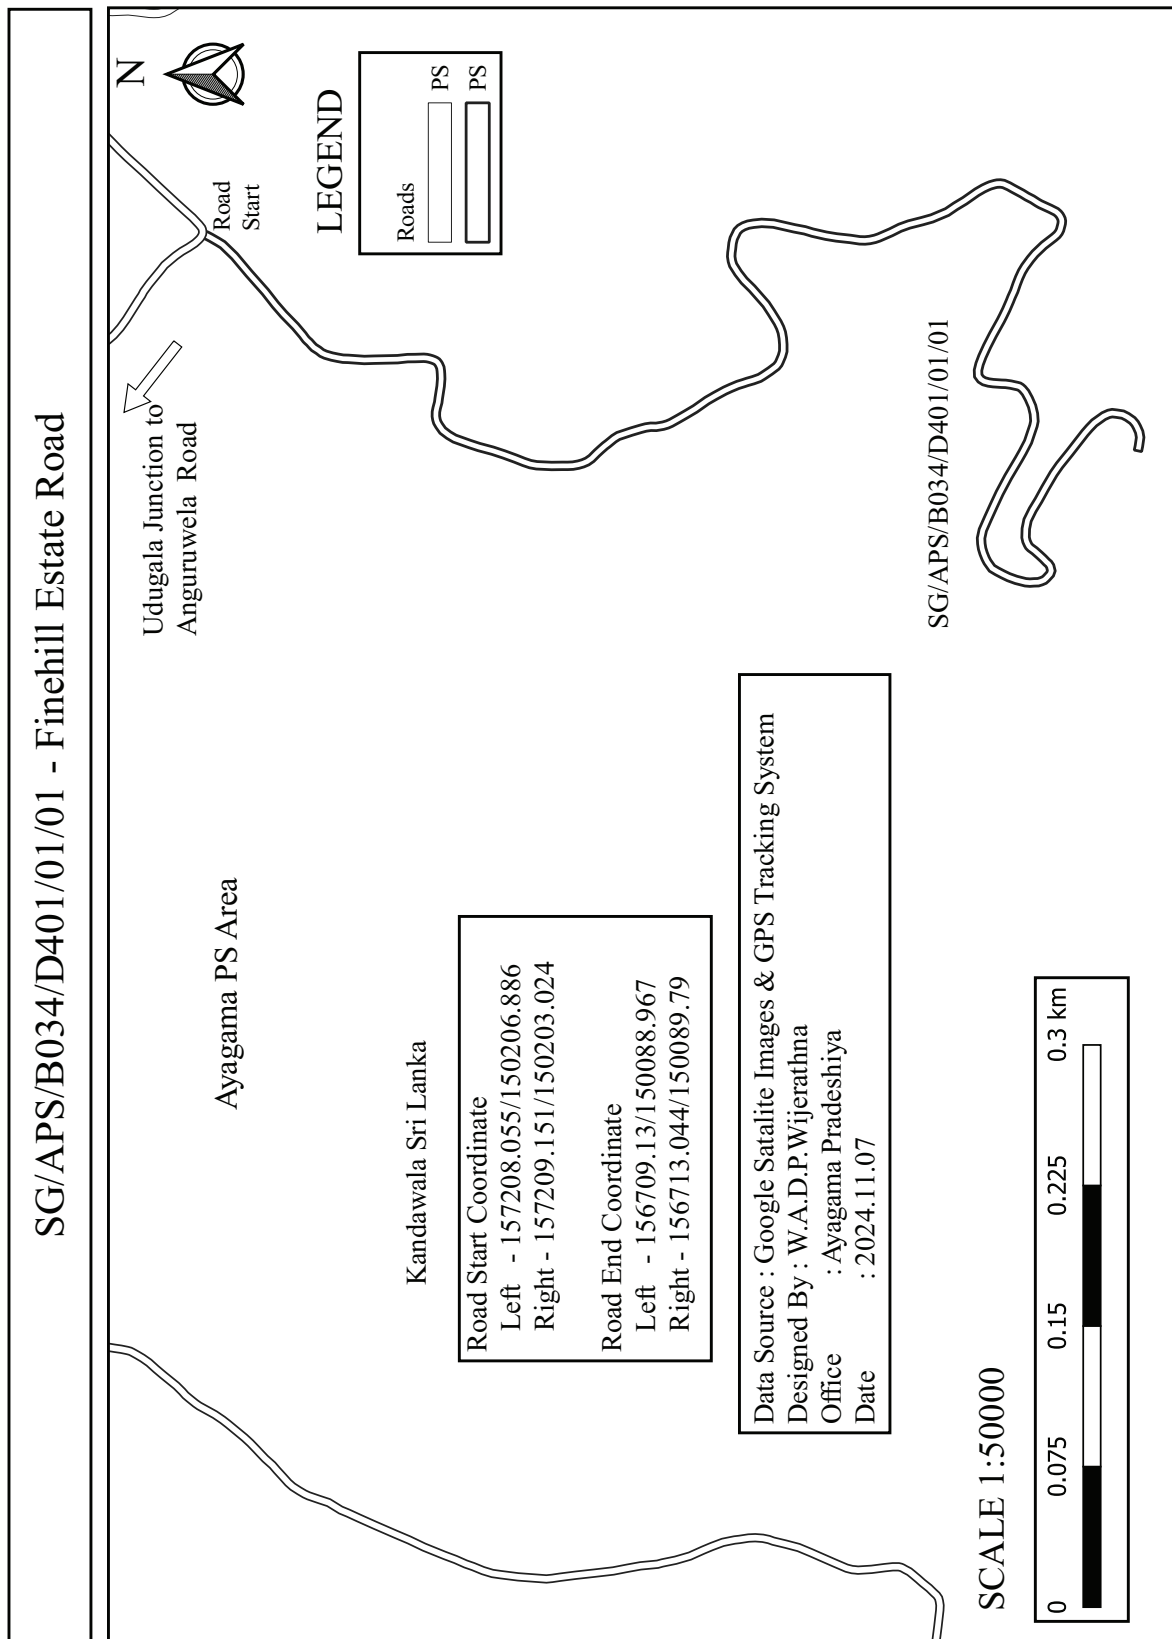


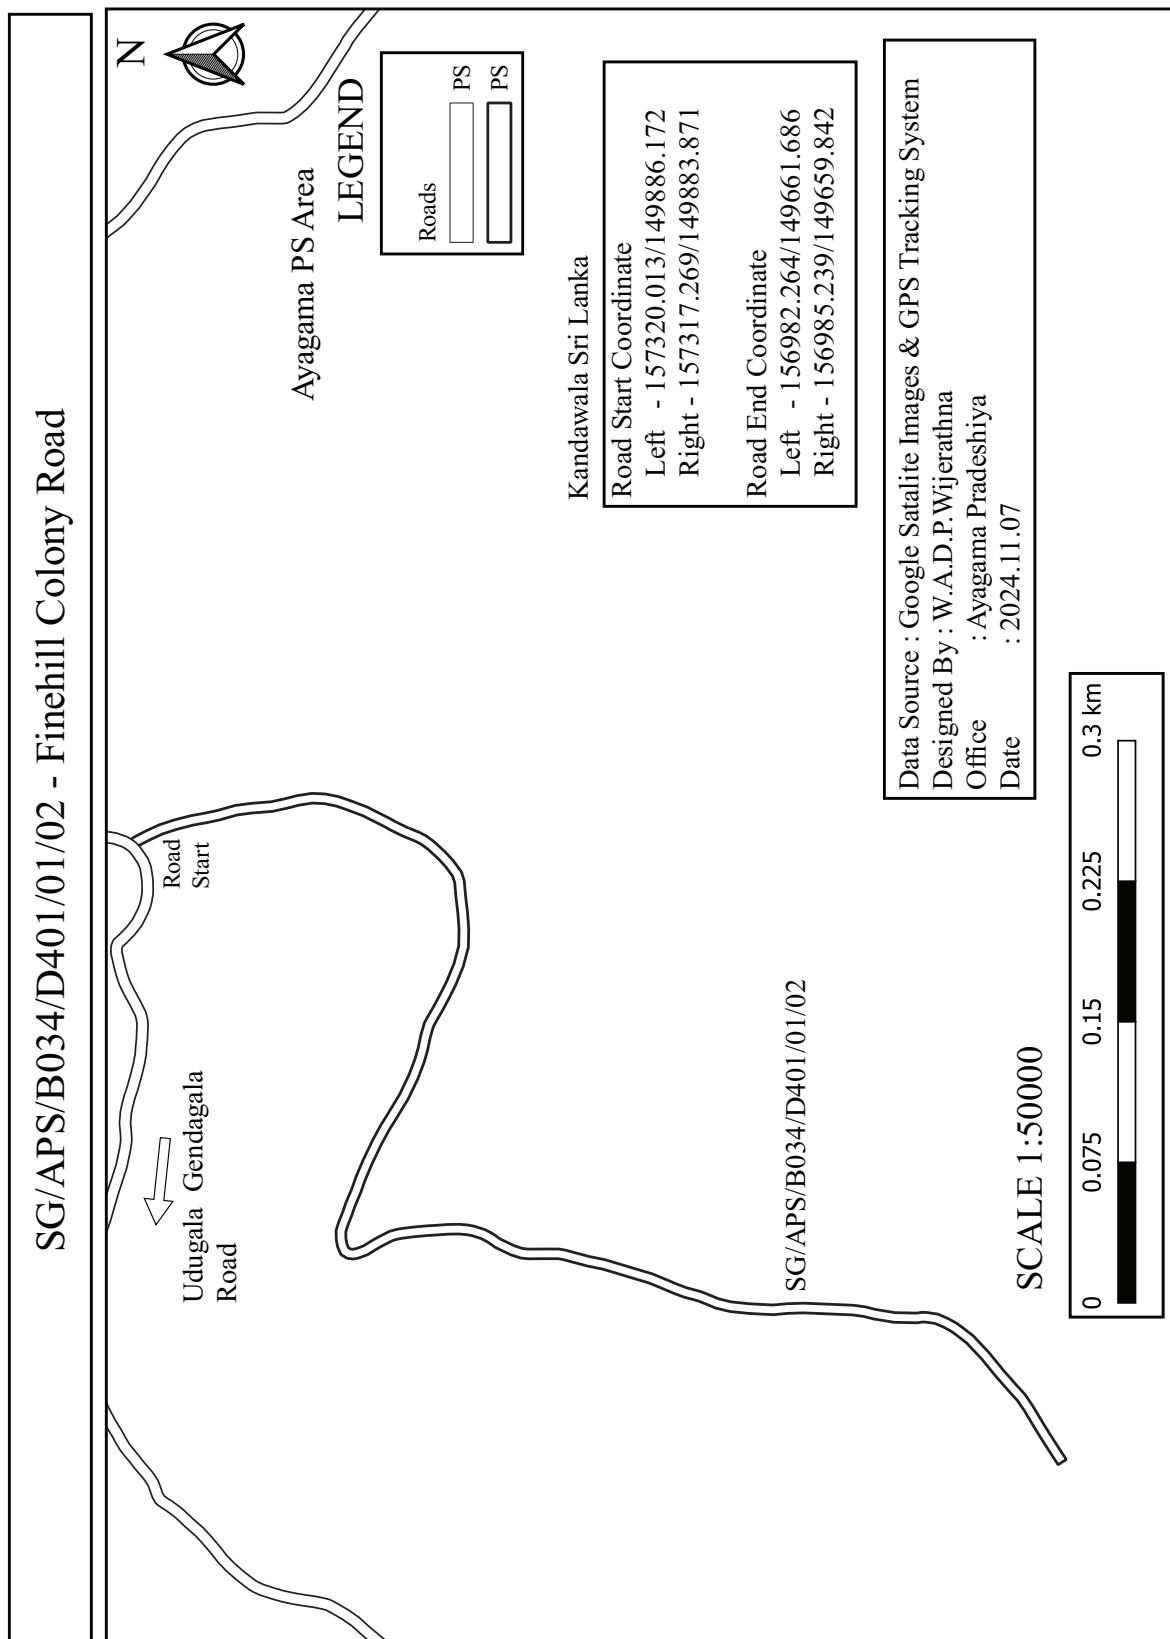


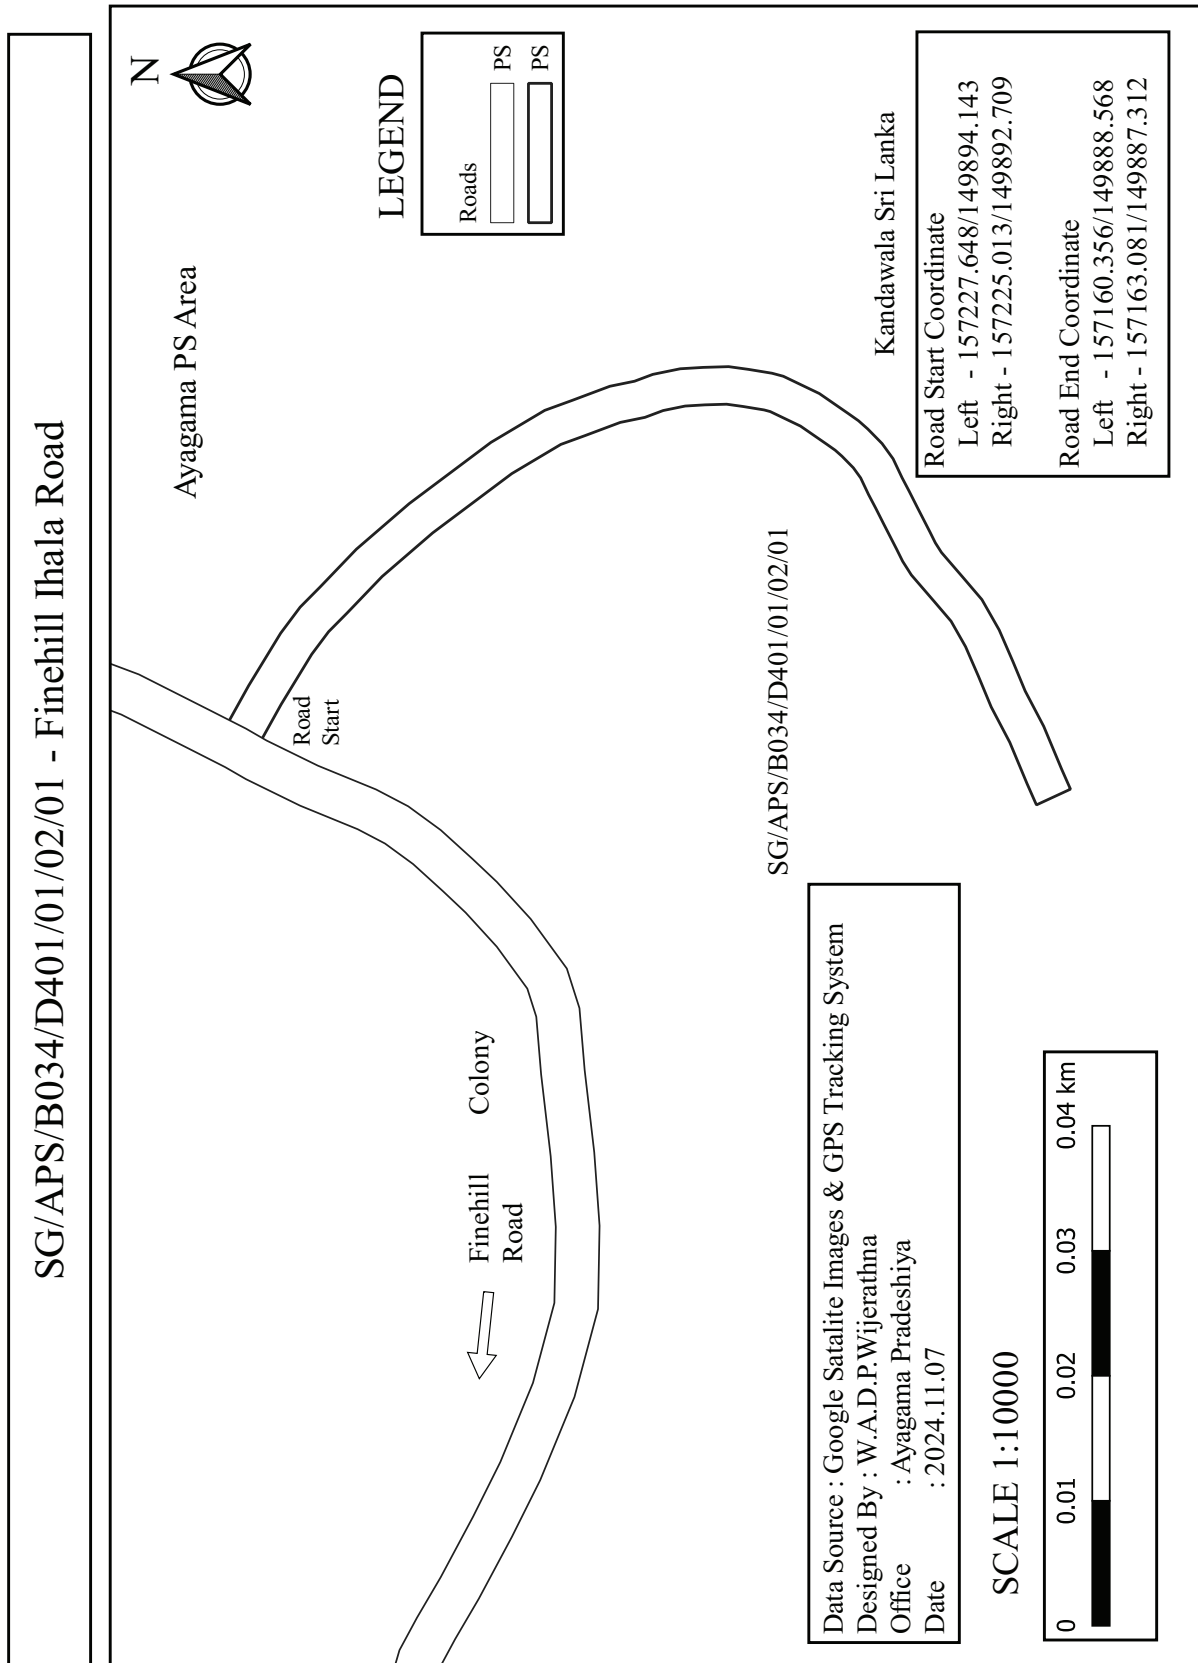


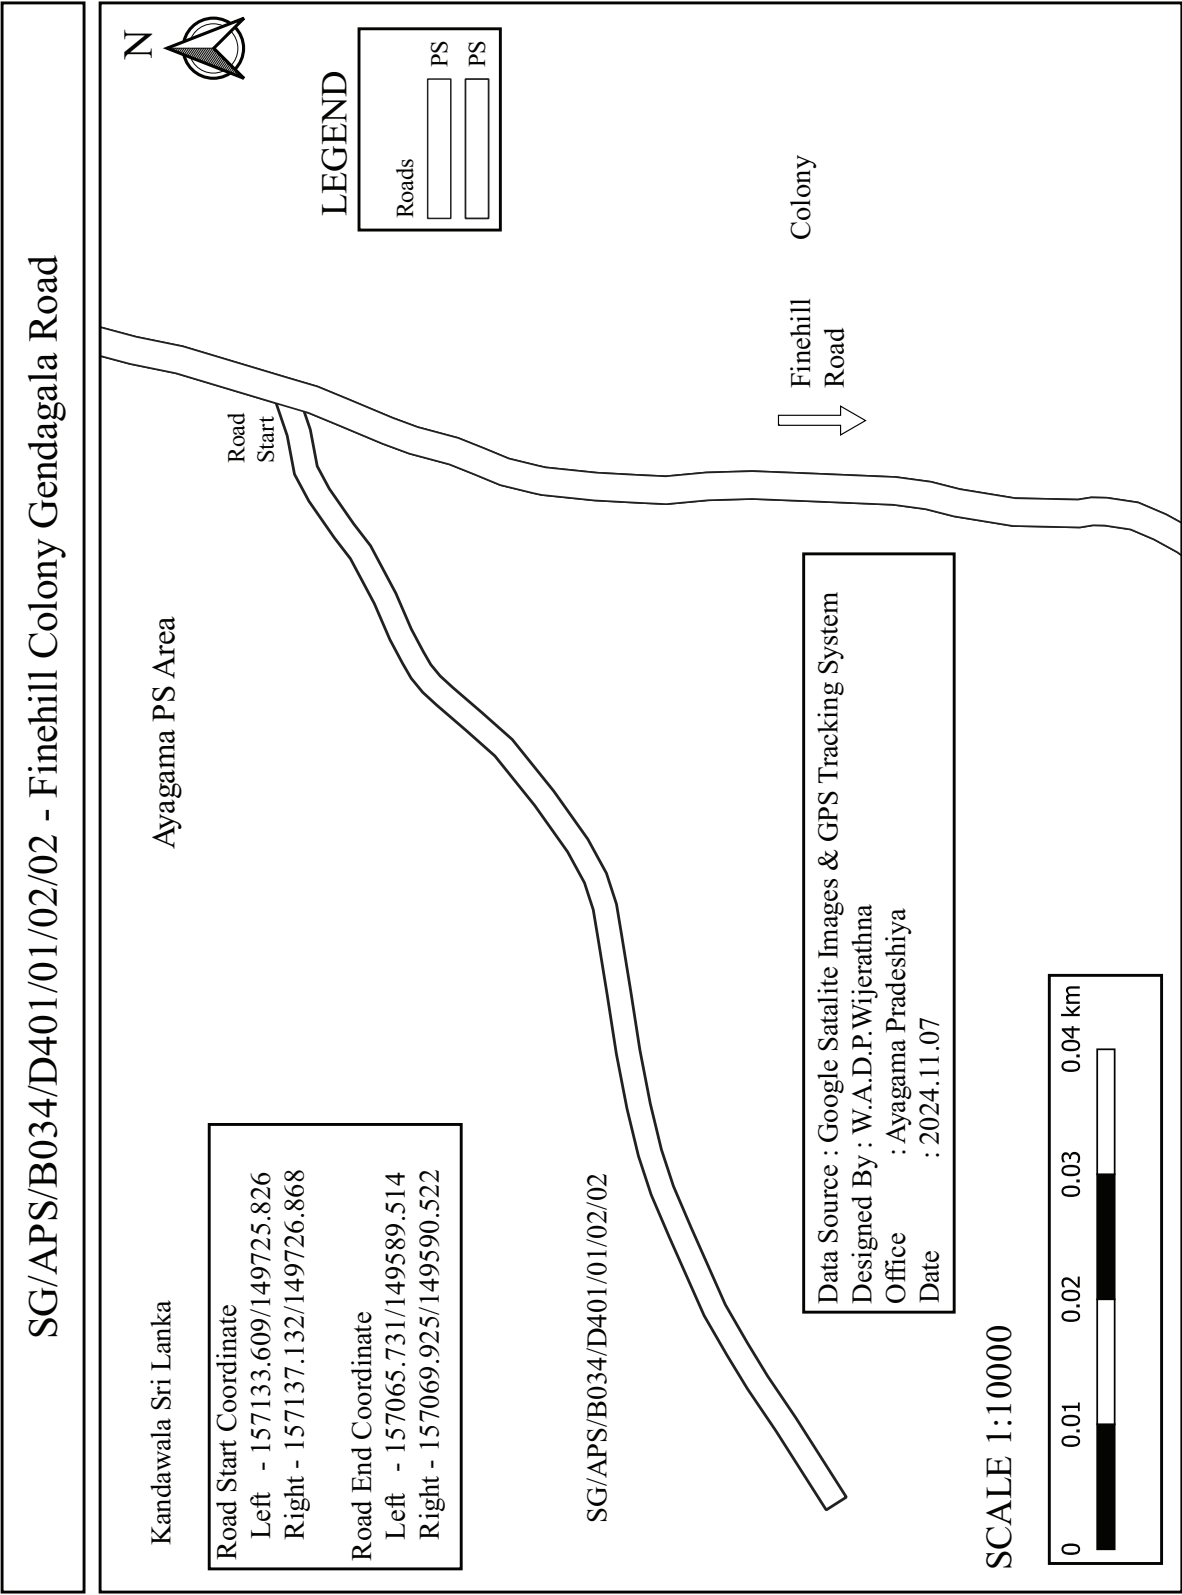


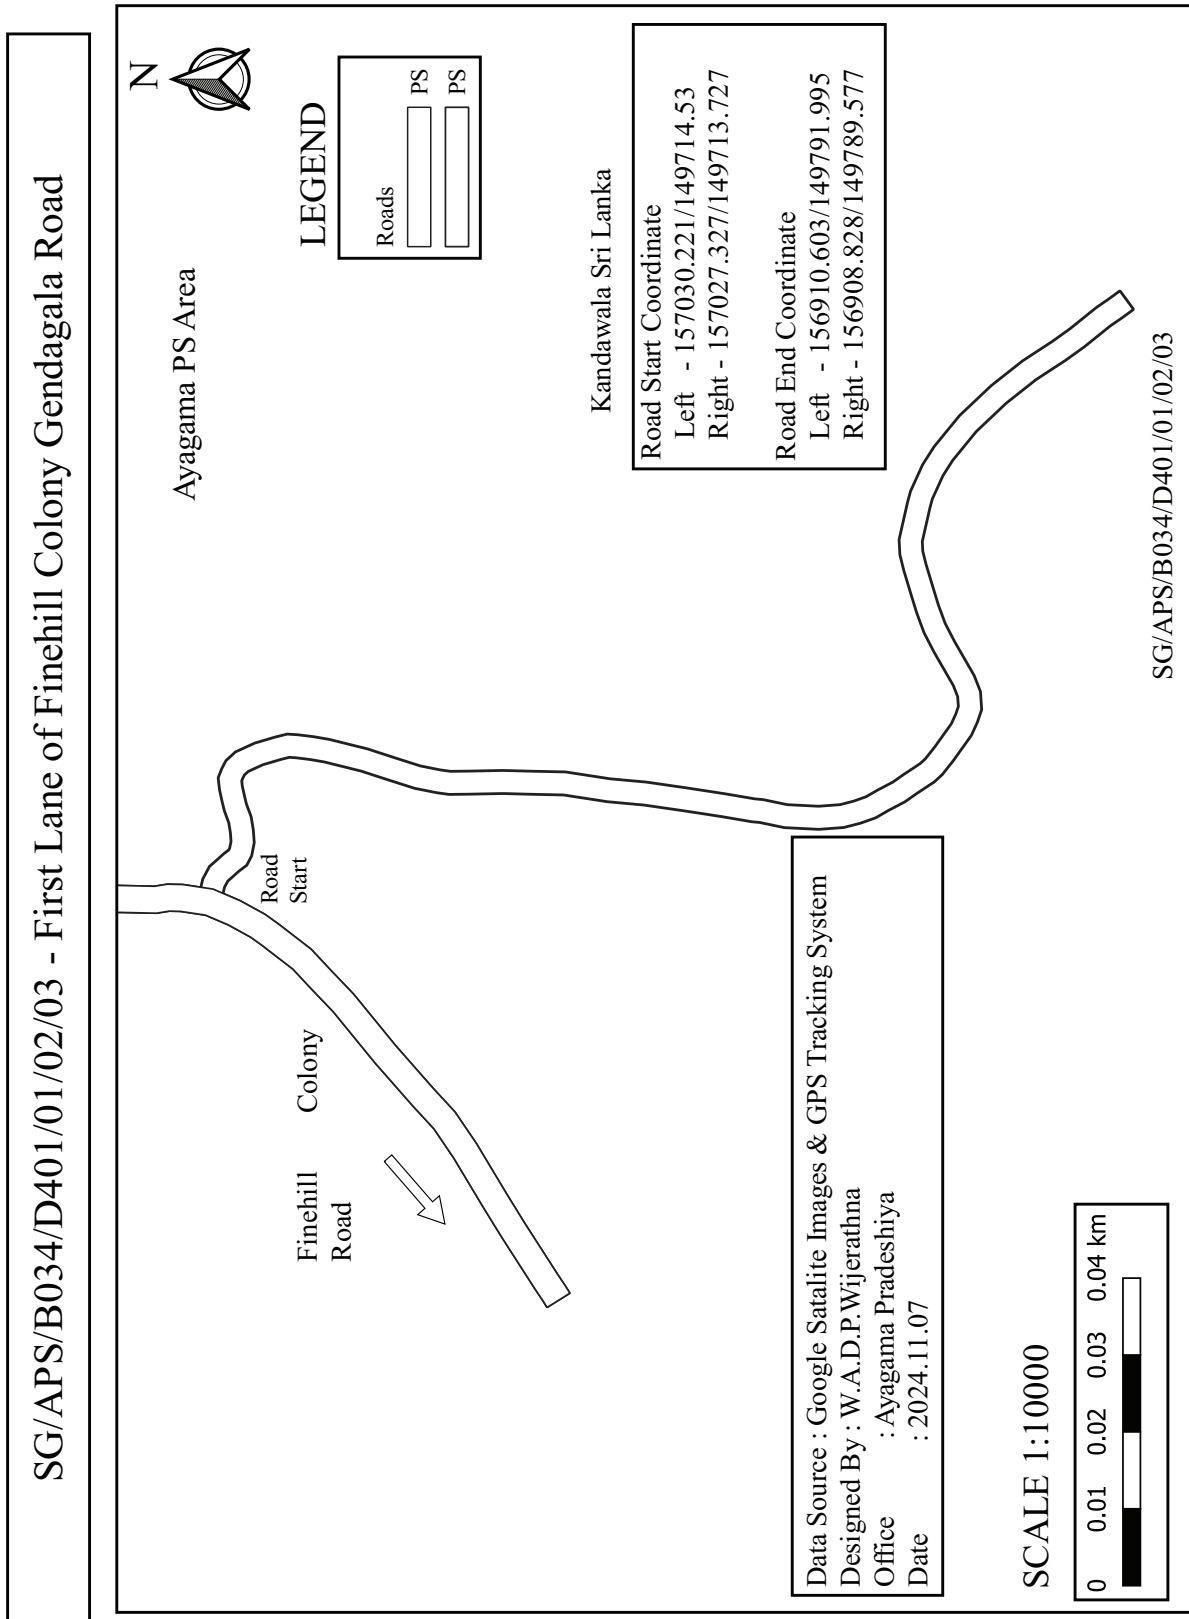


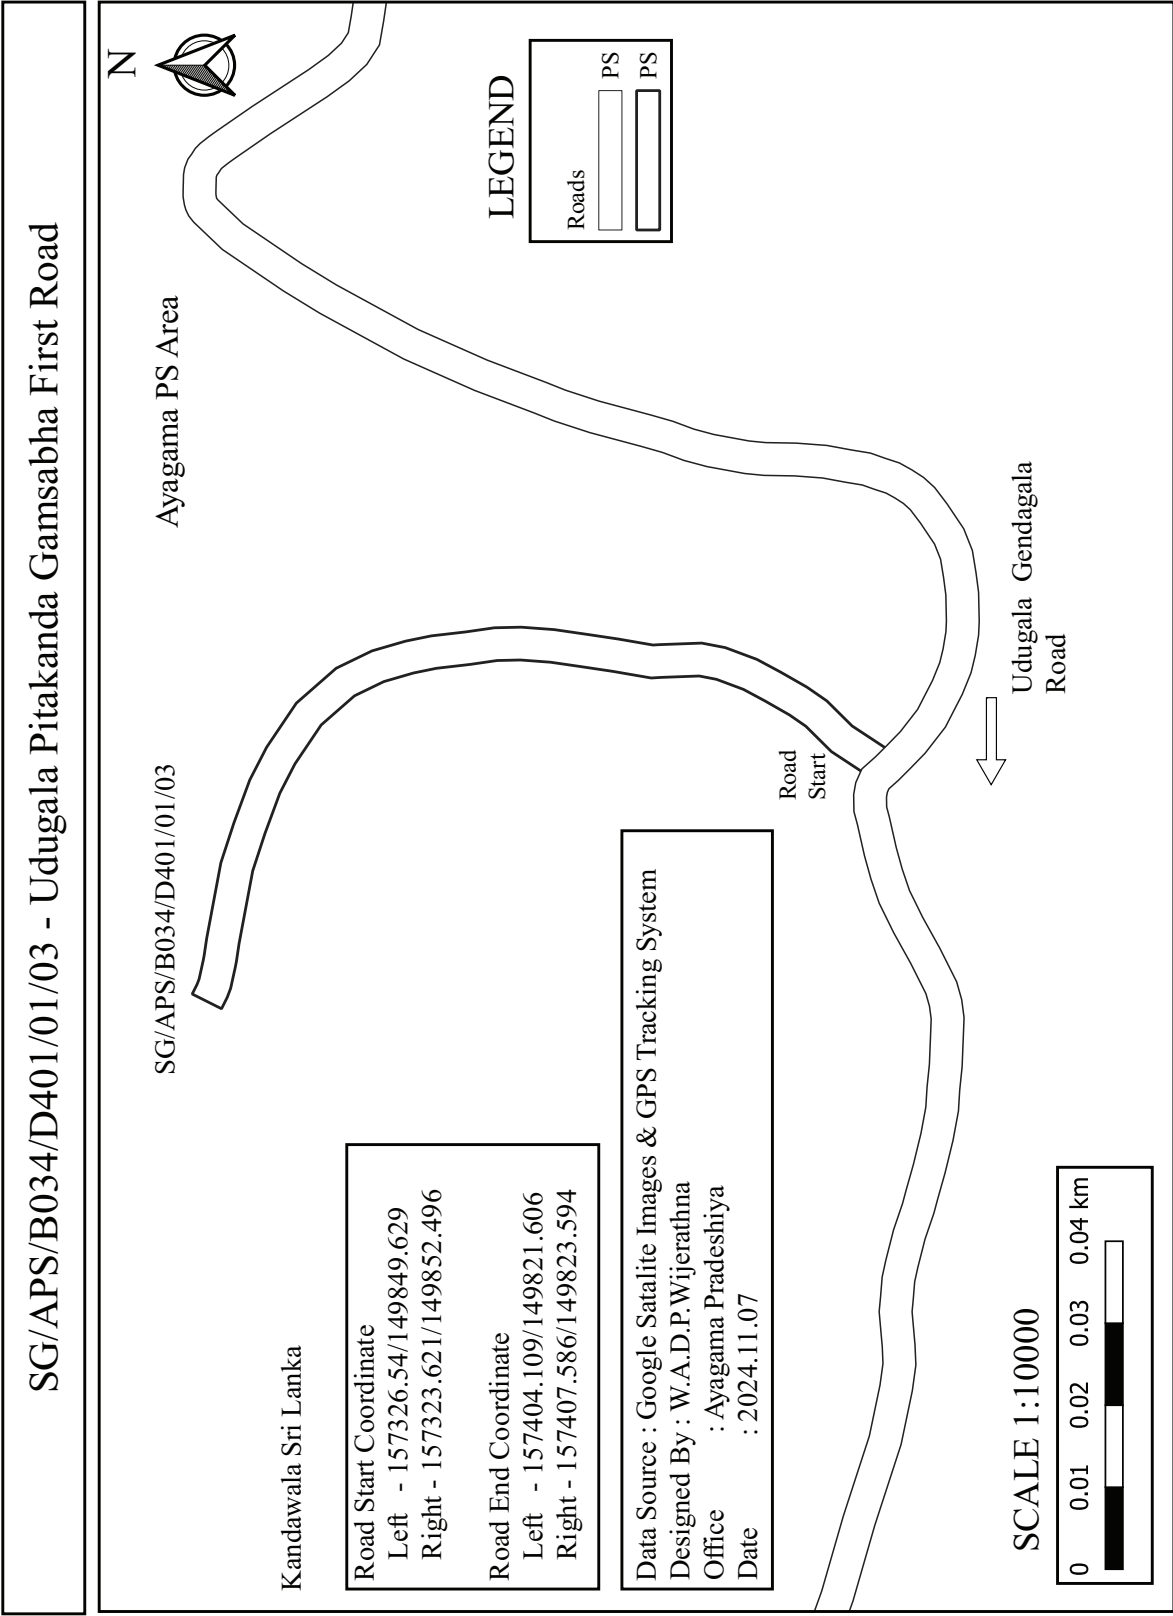

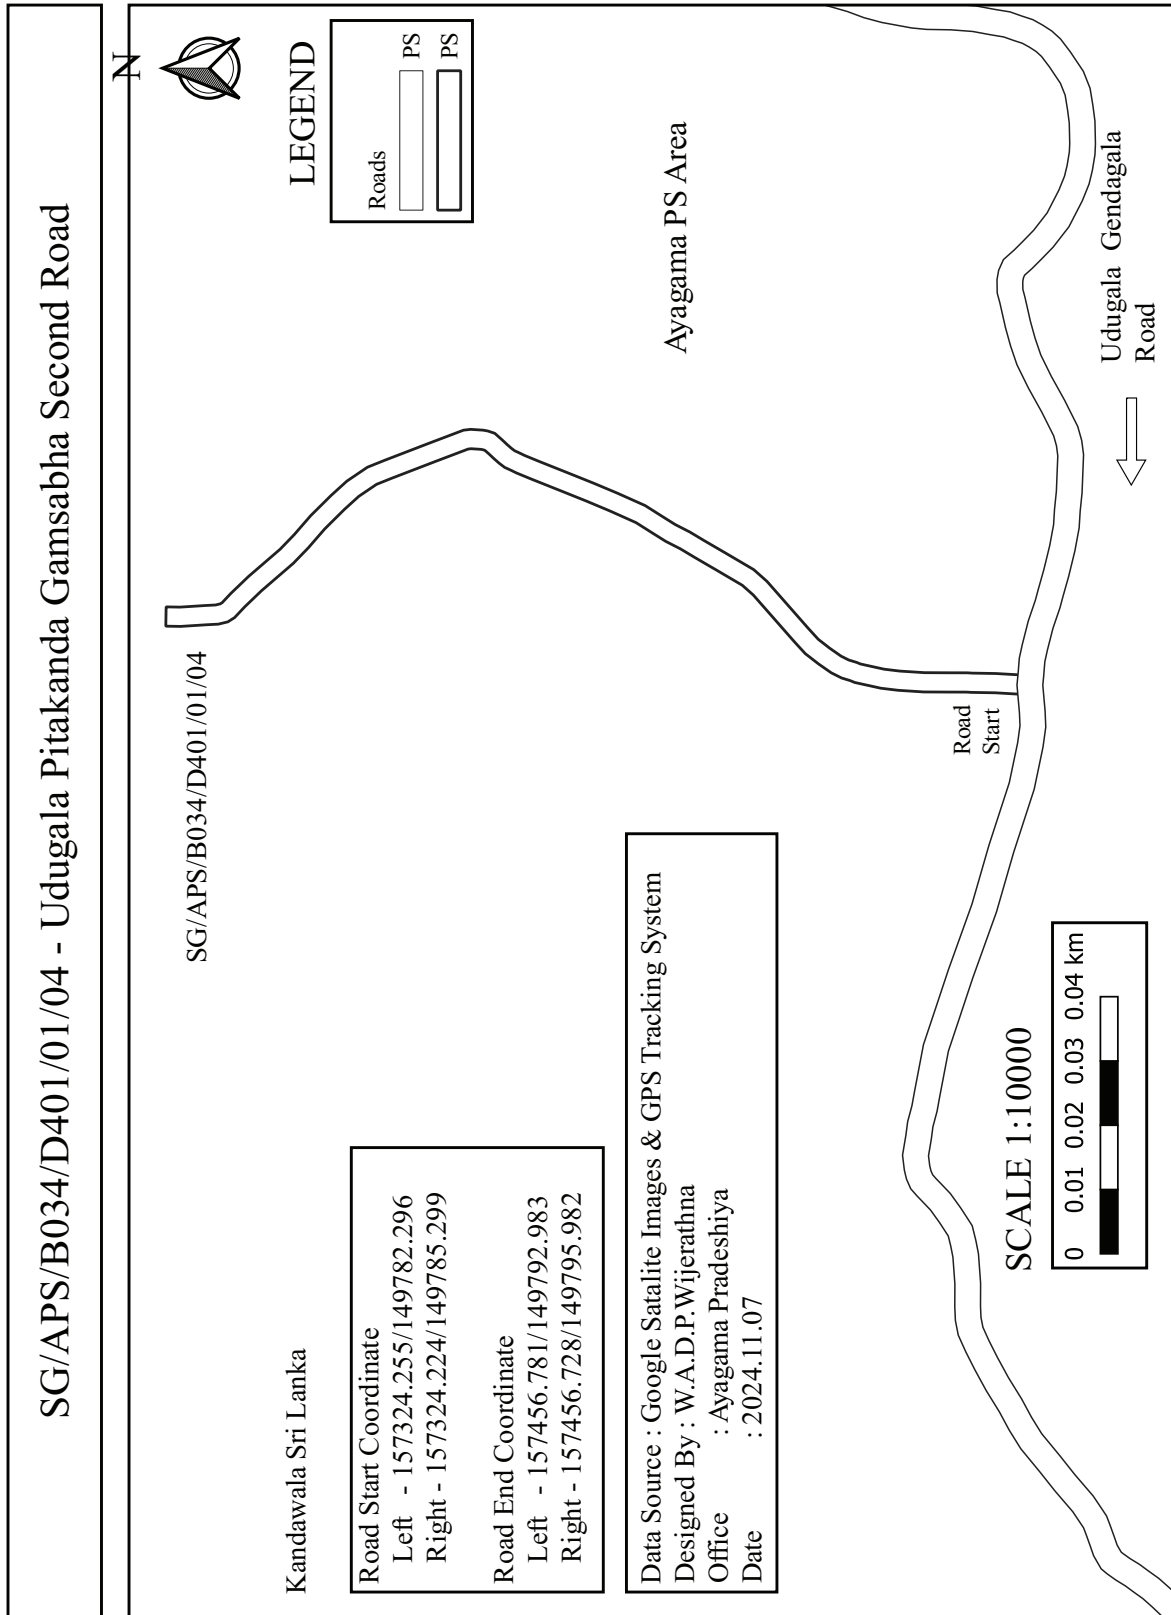


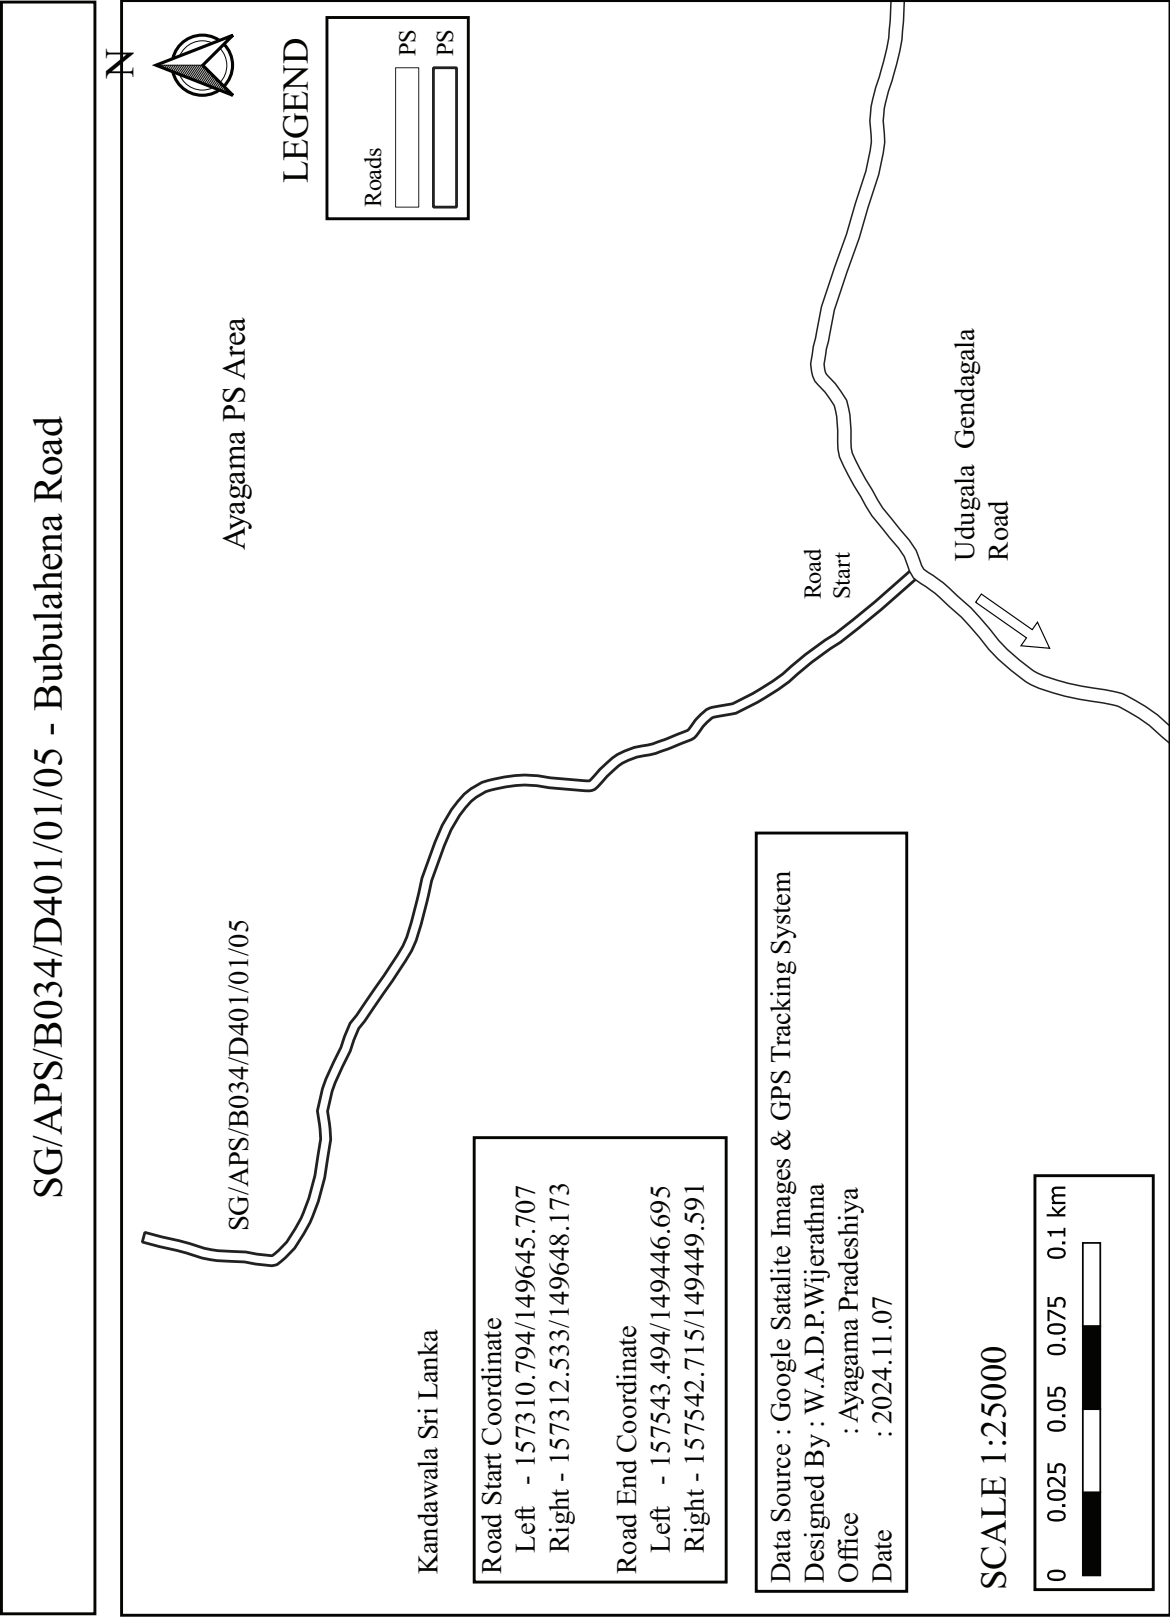


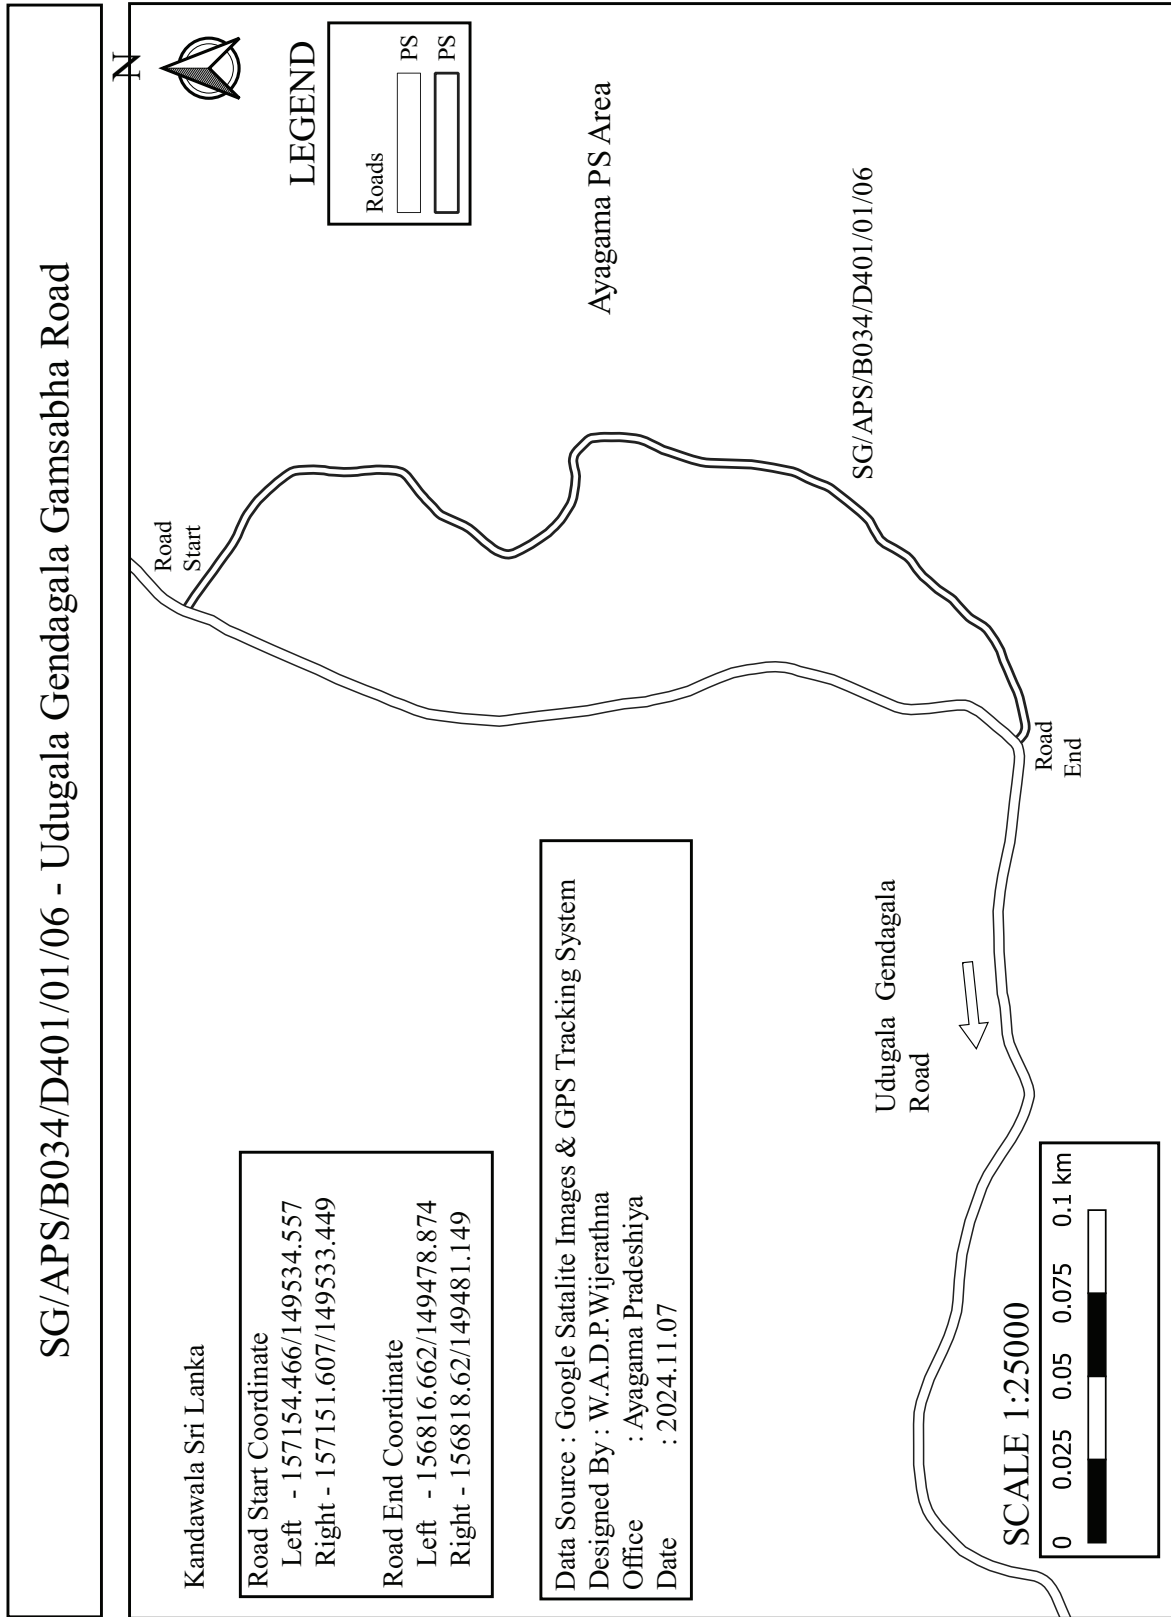


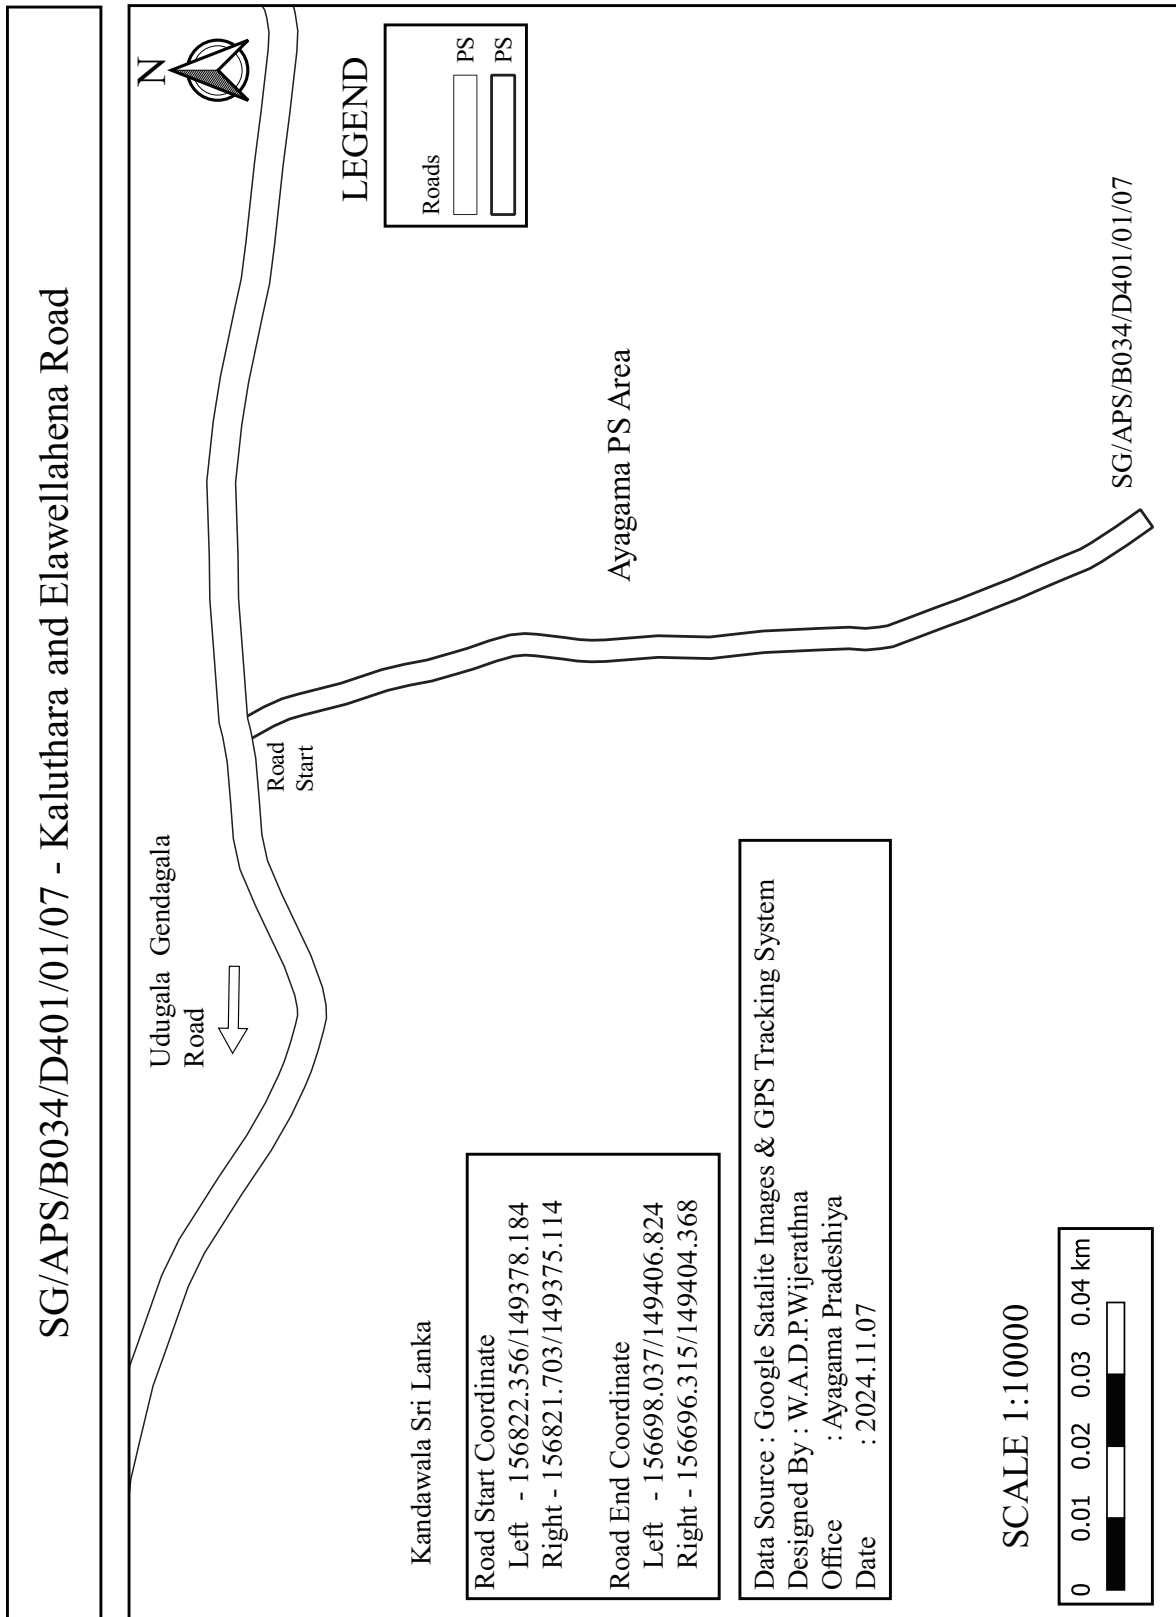

SG/APS/B034/D401/01/08 - First Lane of Udugala Gendagala Road

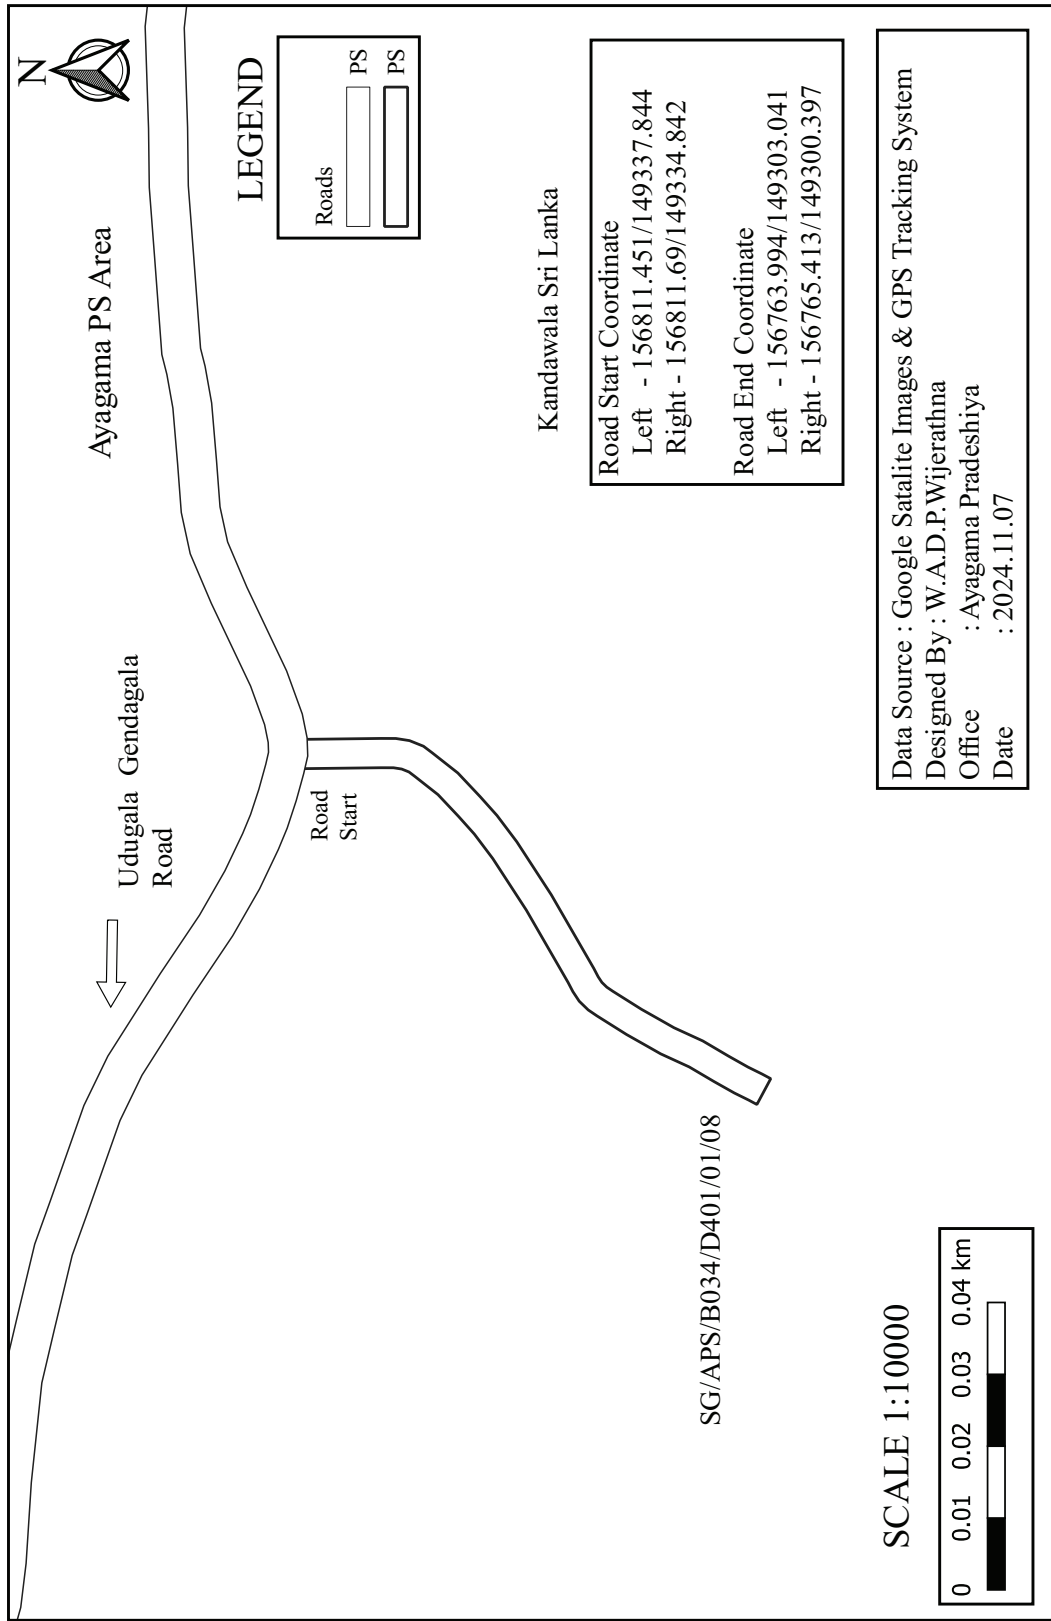

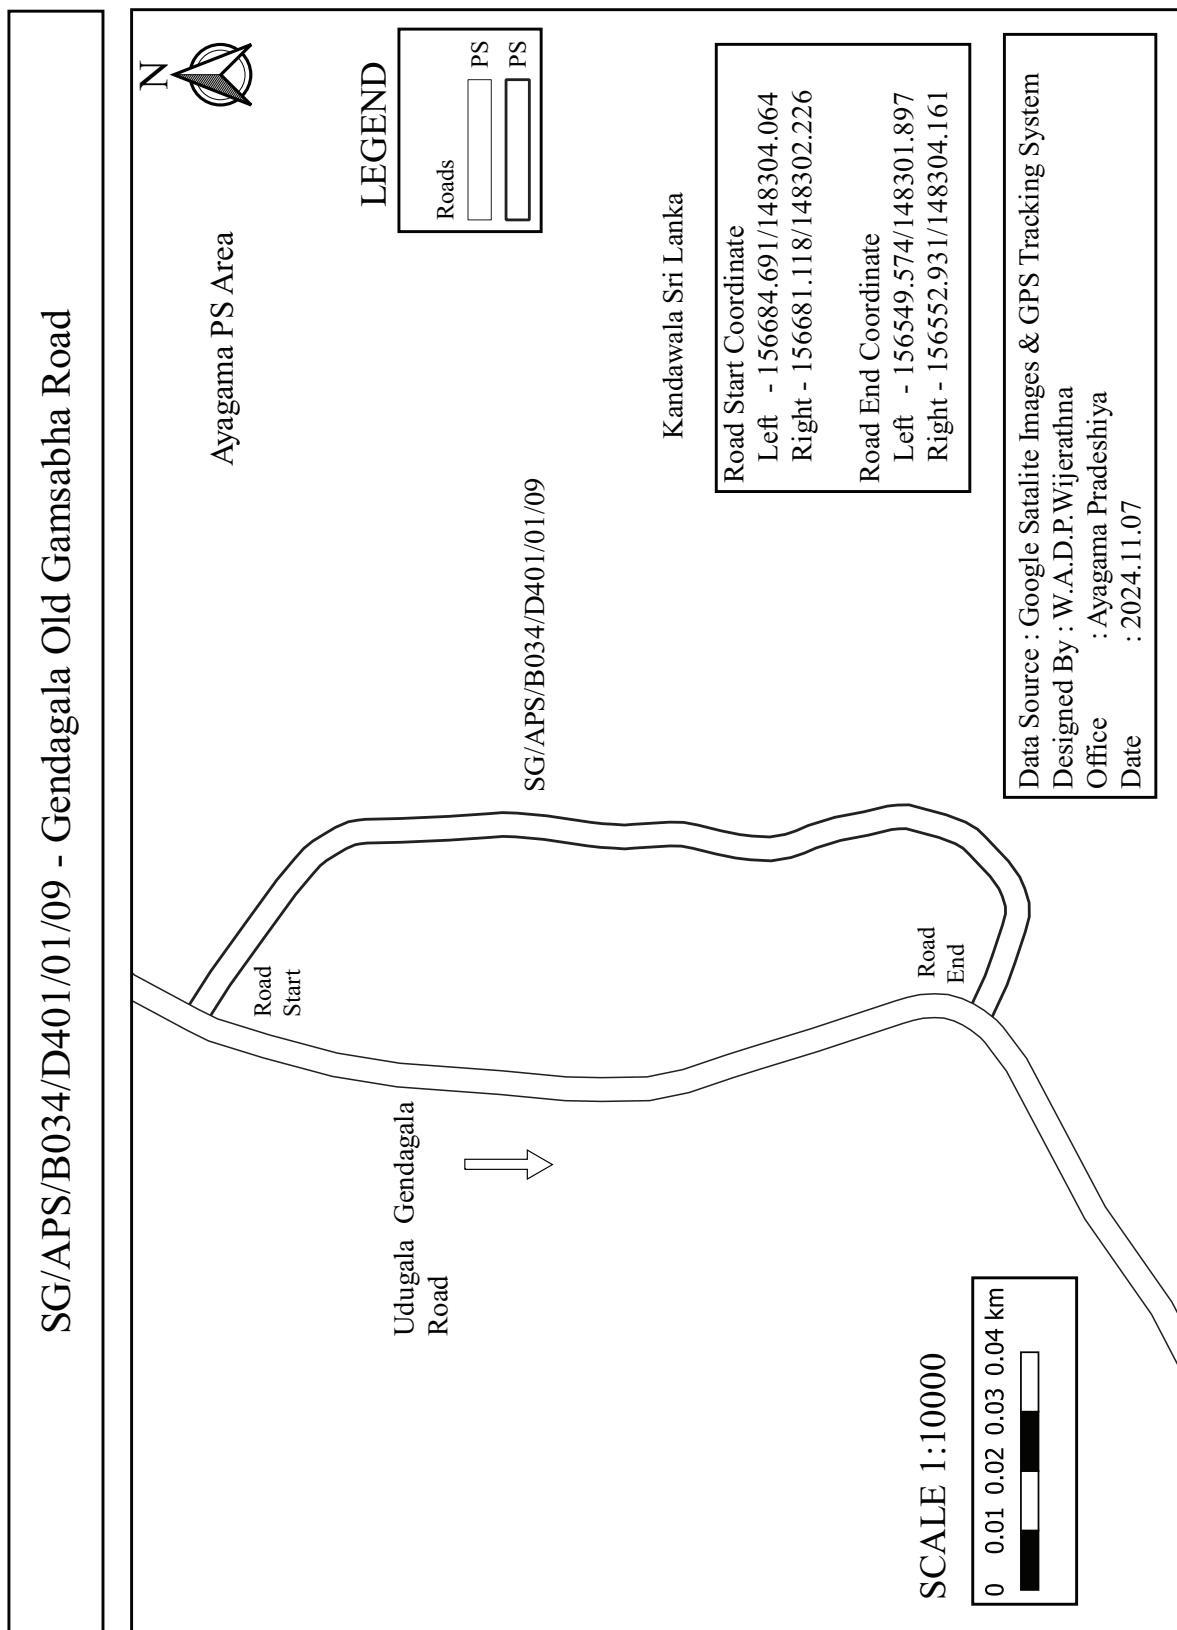


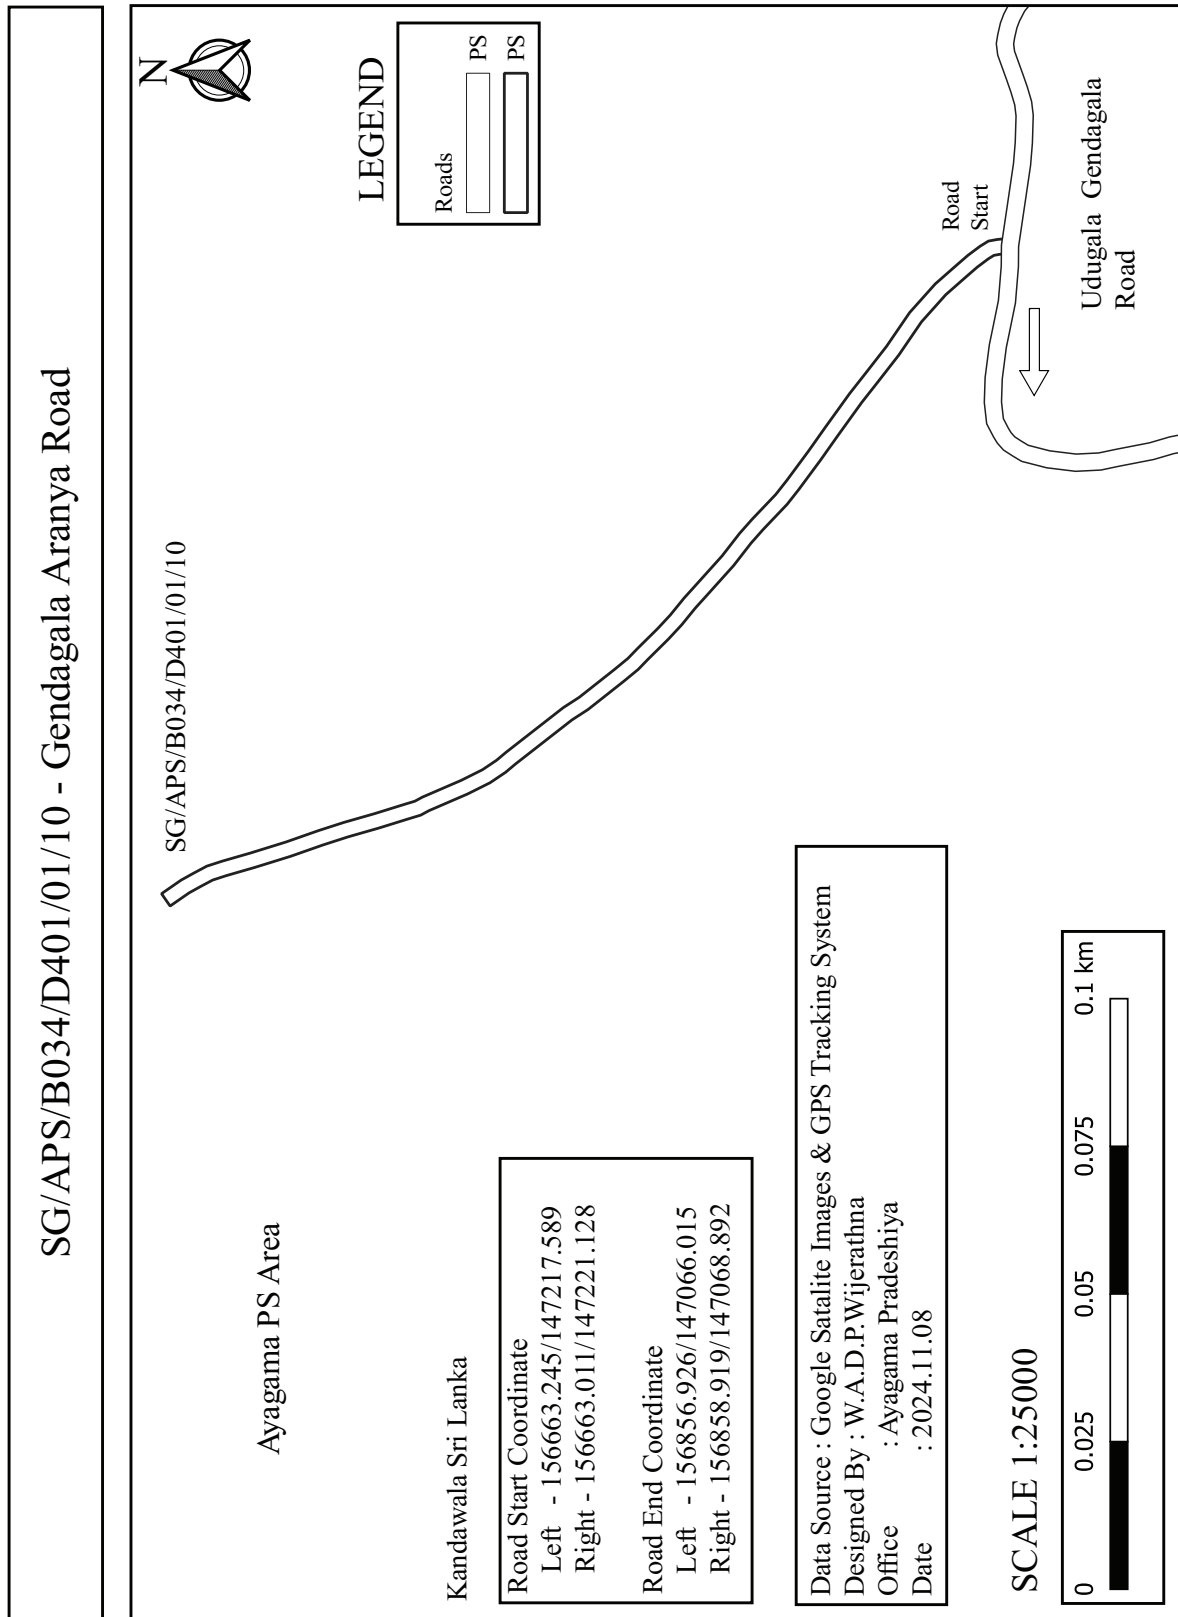


Data Source : Google Satalite Images & GPS Tracking System
 Designed By : W.A.D.P.Wijerathna
 Office : Ayagama Pradeshiya
 Date : 2024.11.08


SCALE 1:25000


0 0.025 0.05 0.075 0.1 km

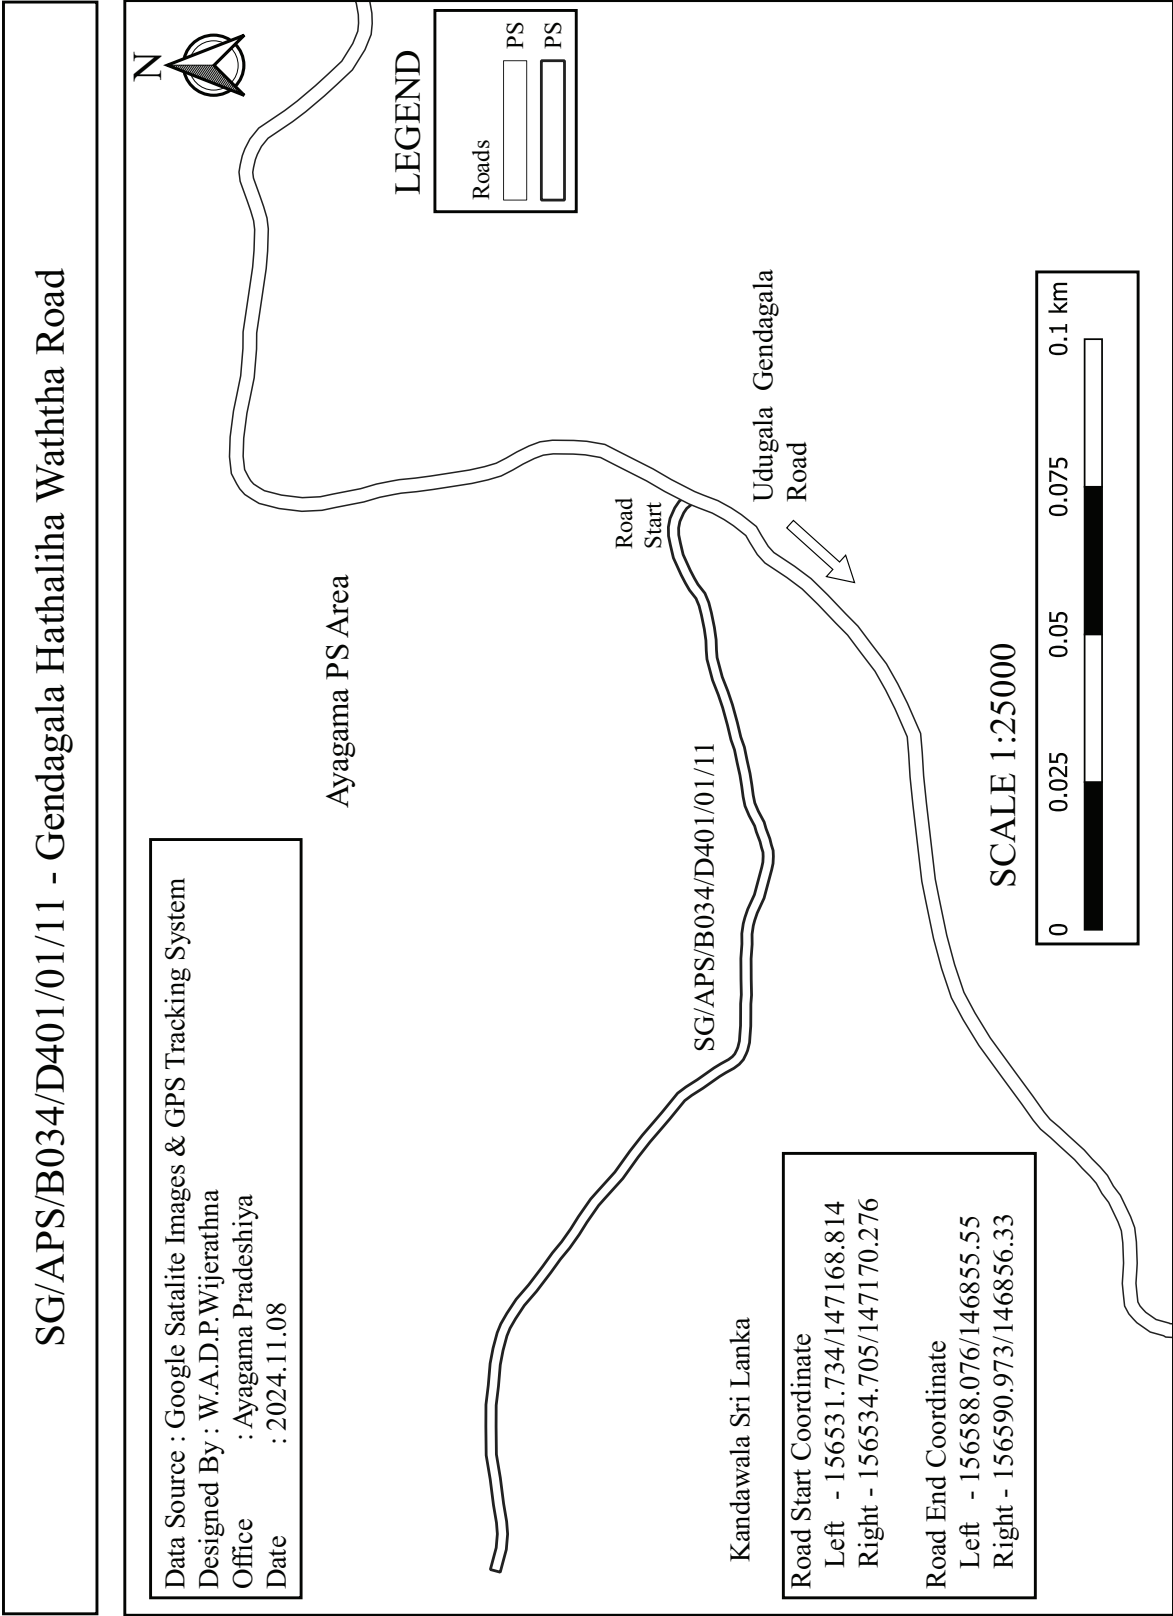



SG/APS/B034/D401/01/12 - Gendagala Millahena Footpath

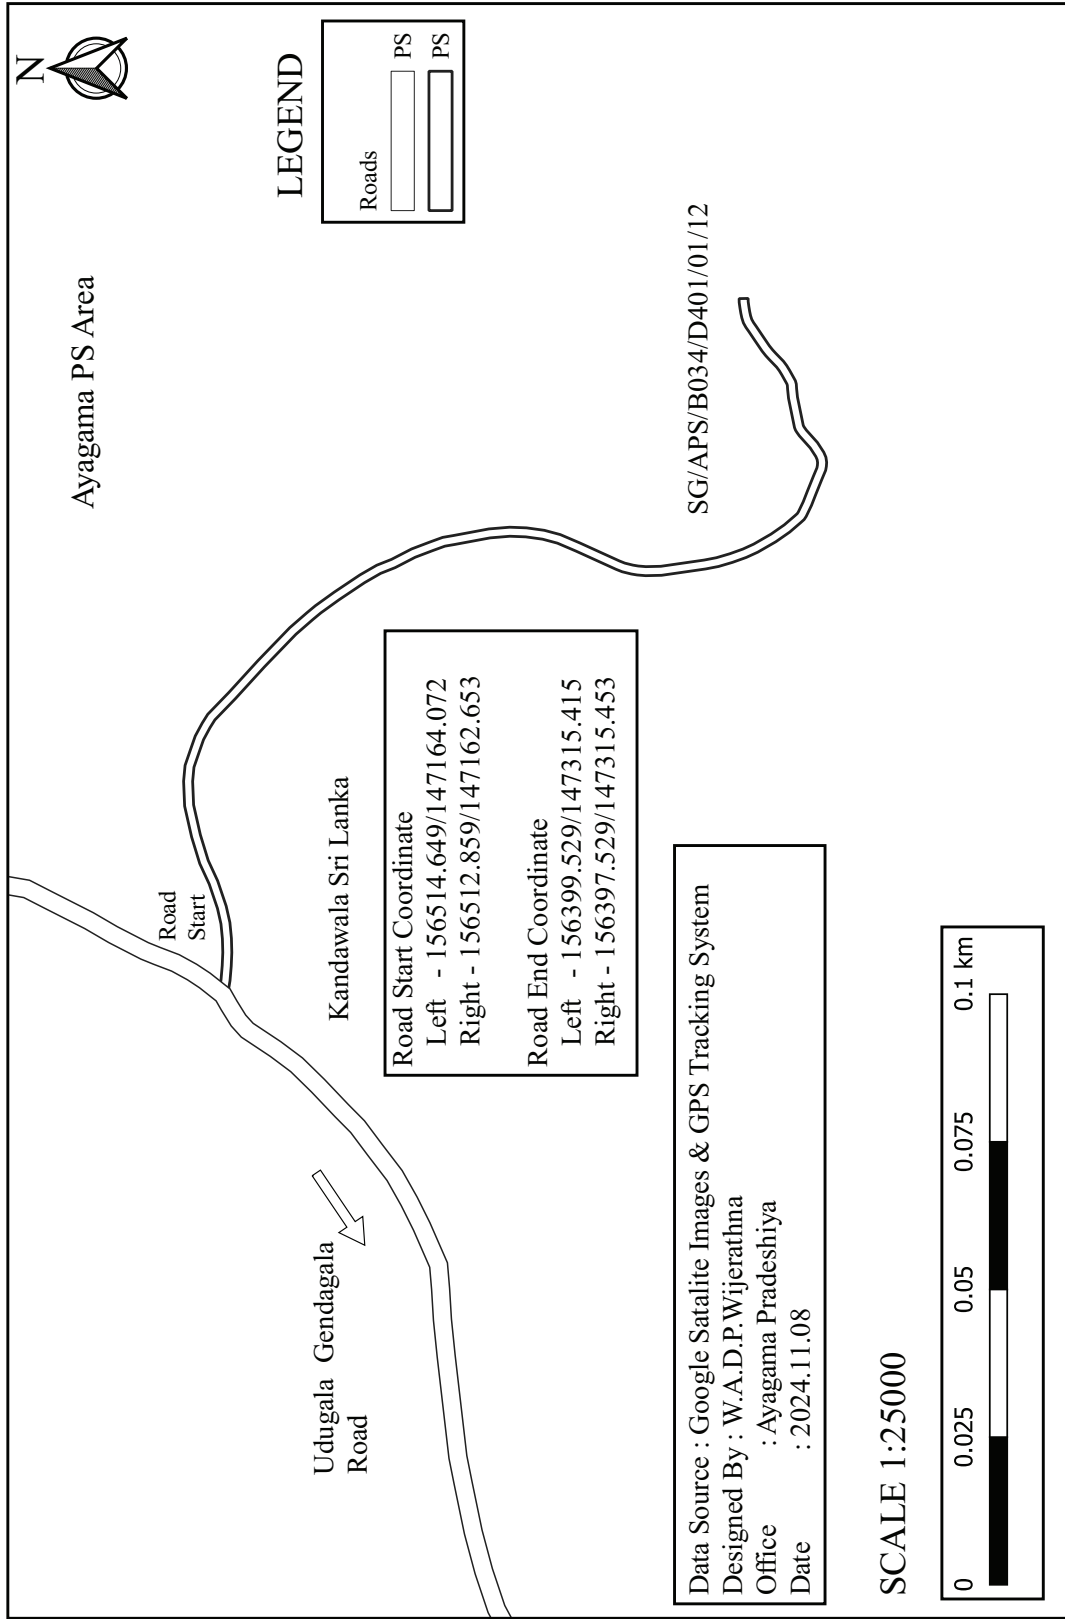


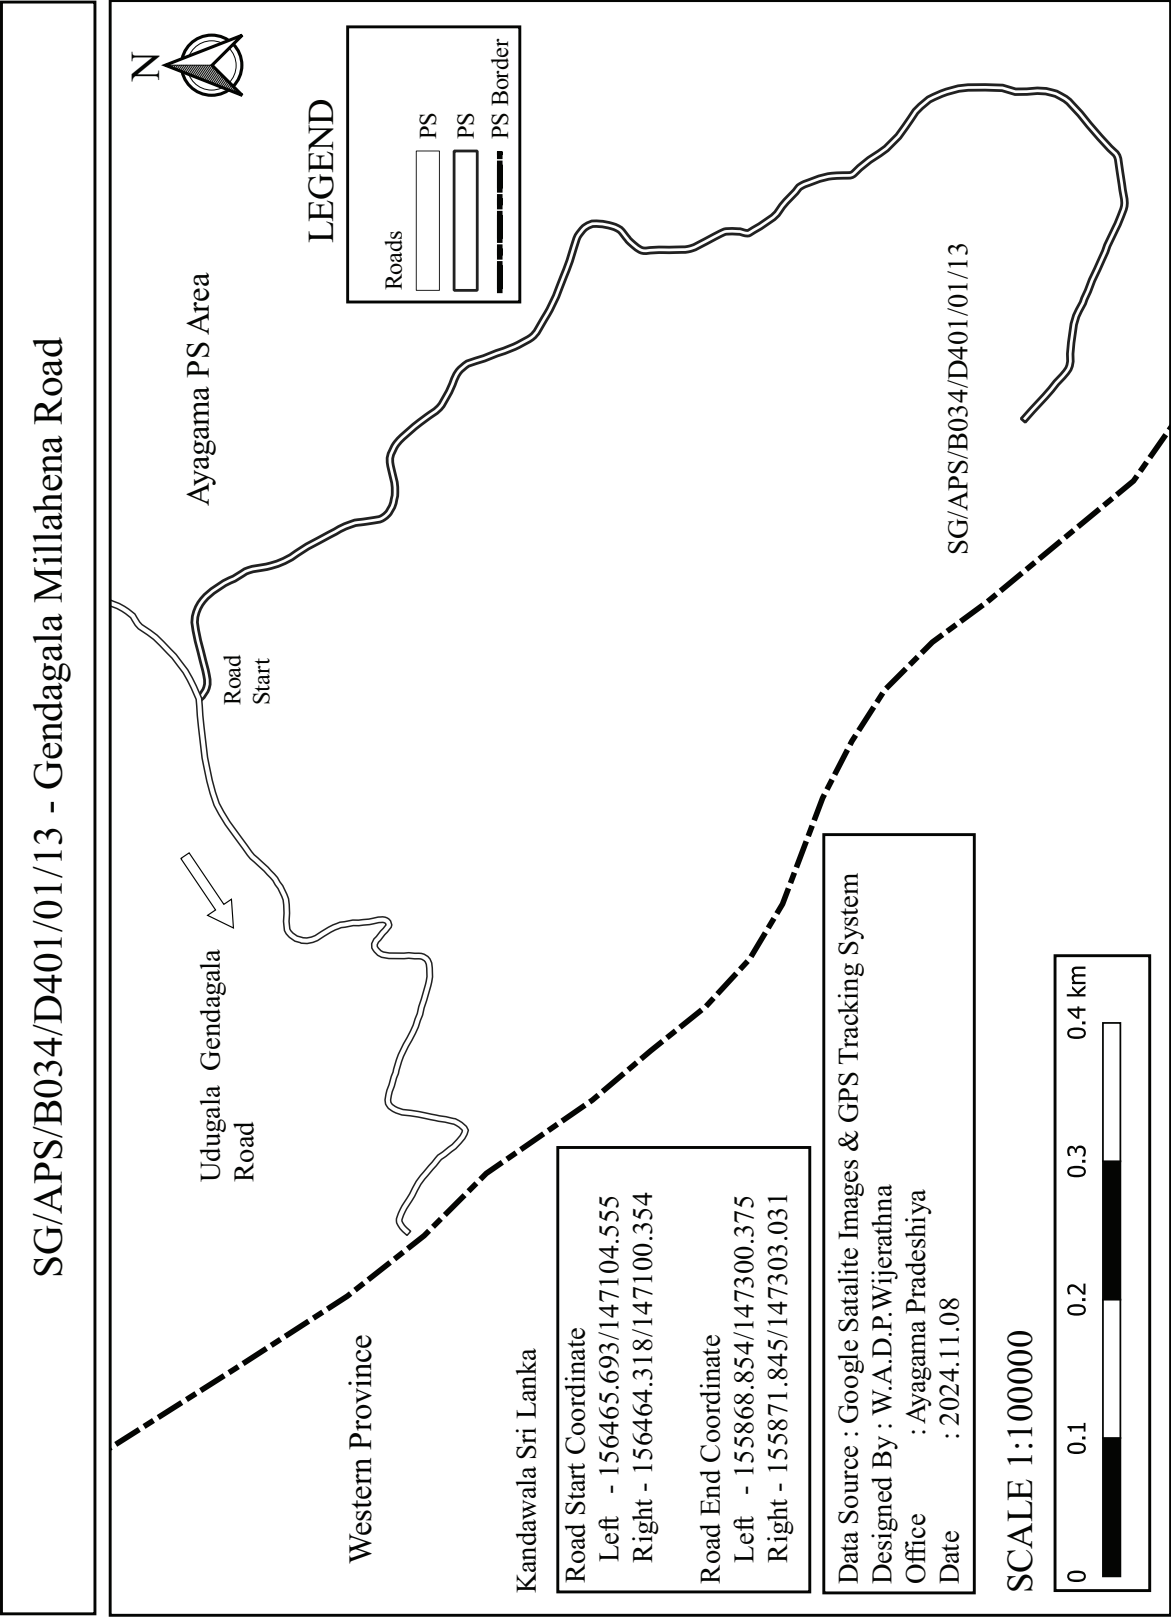


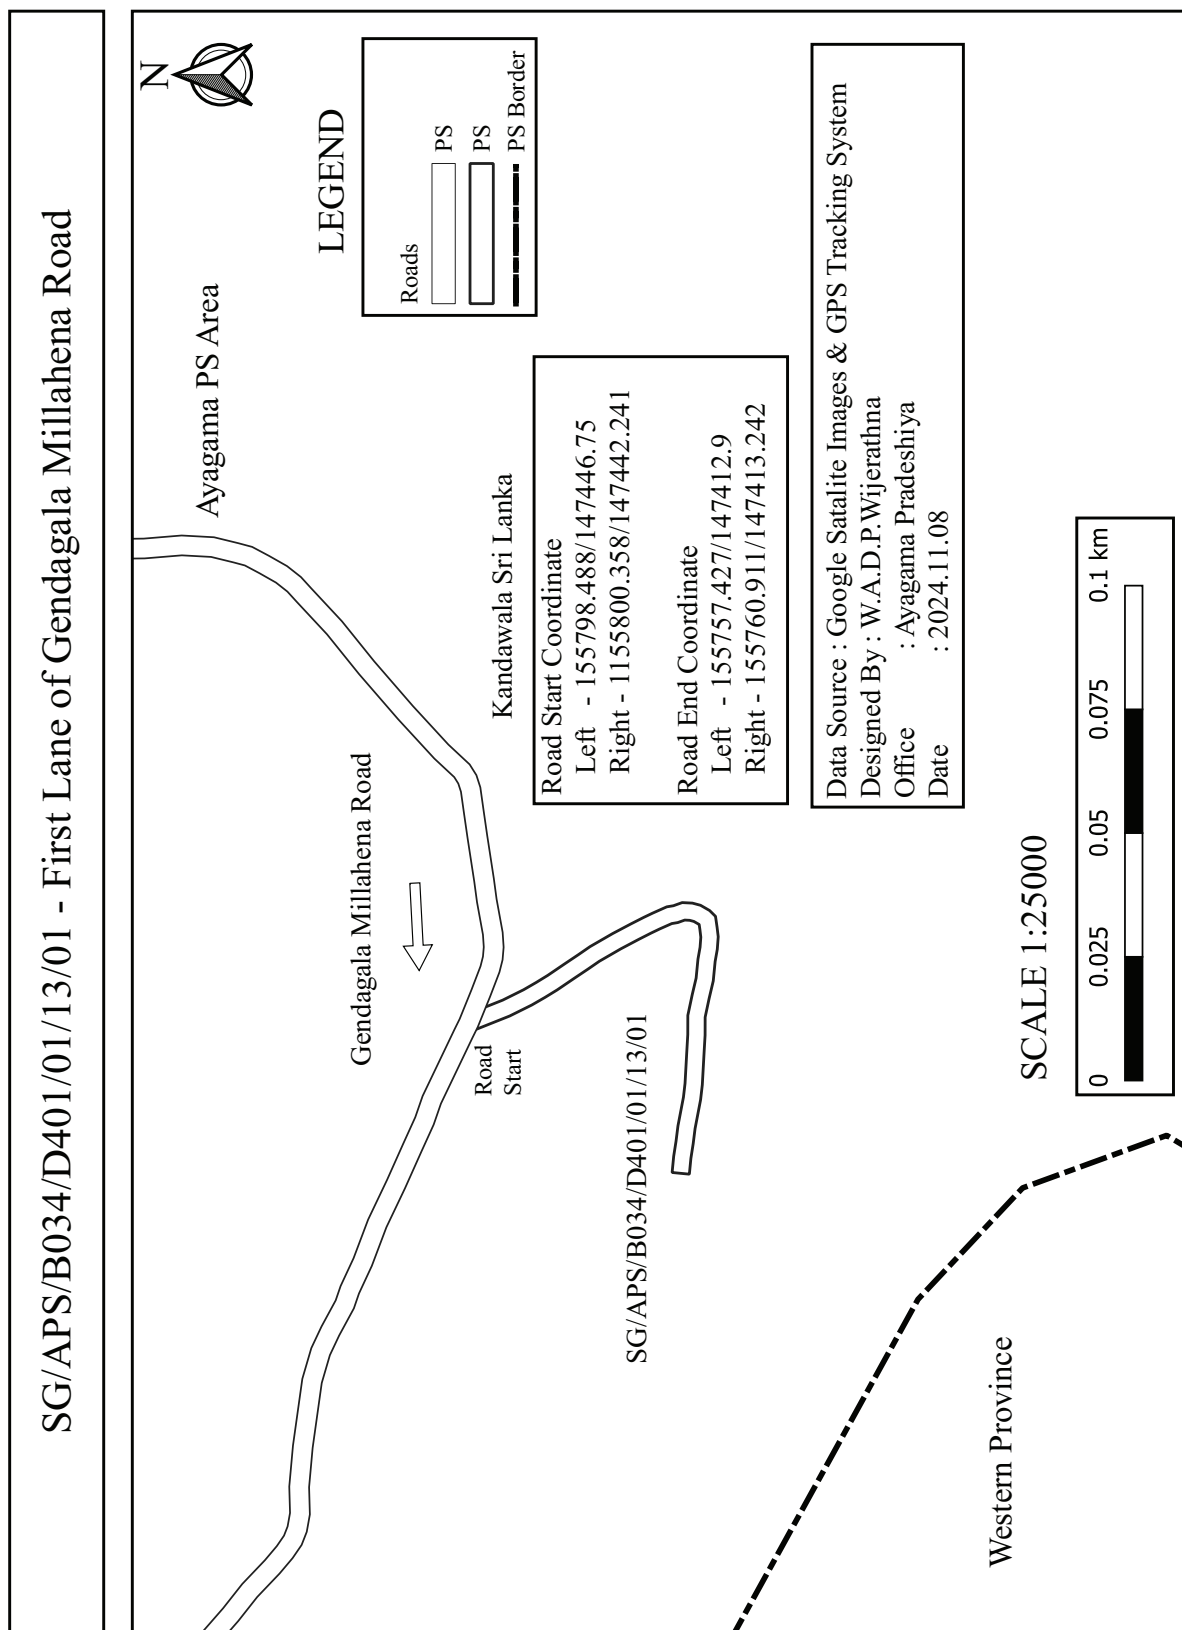


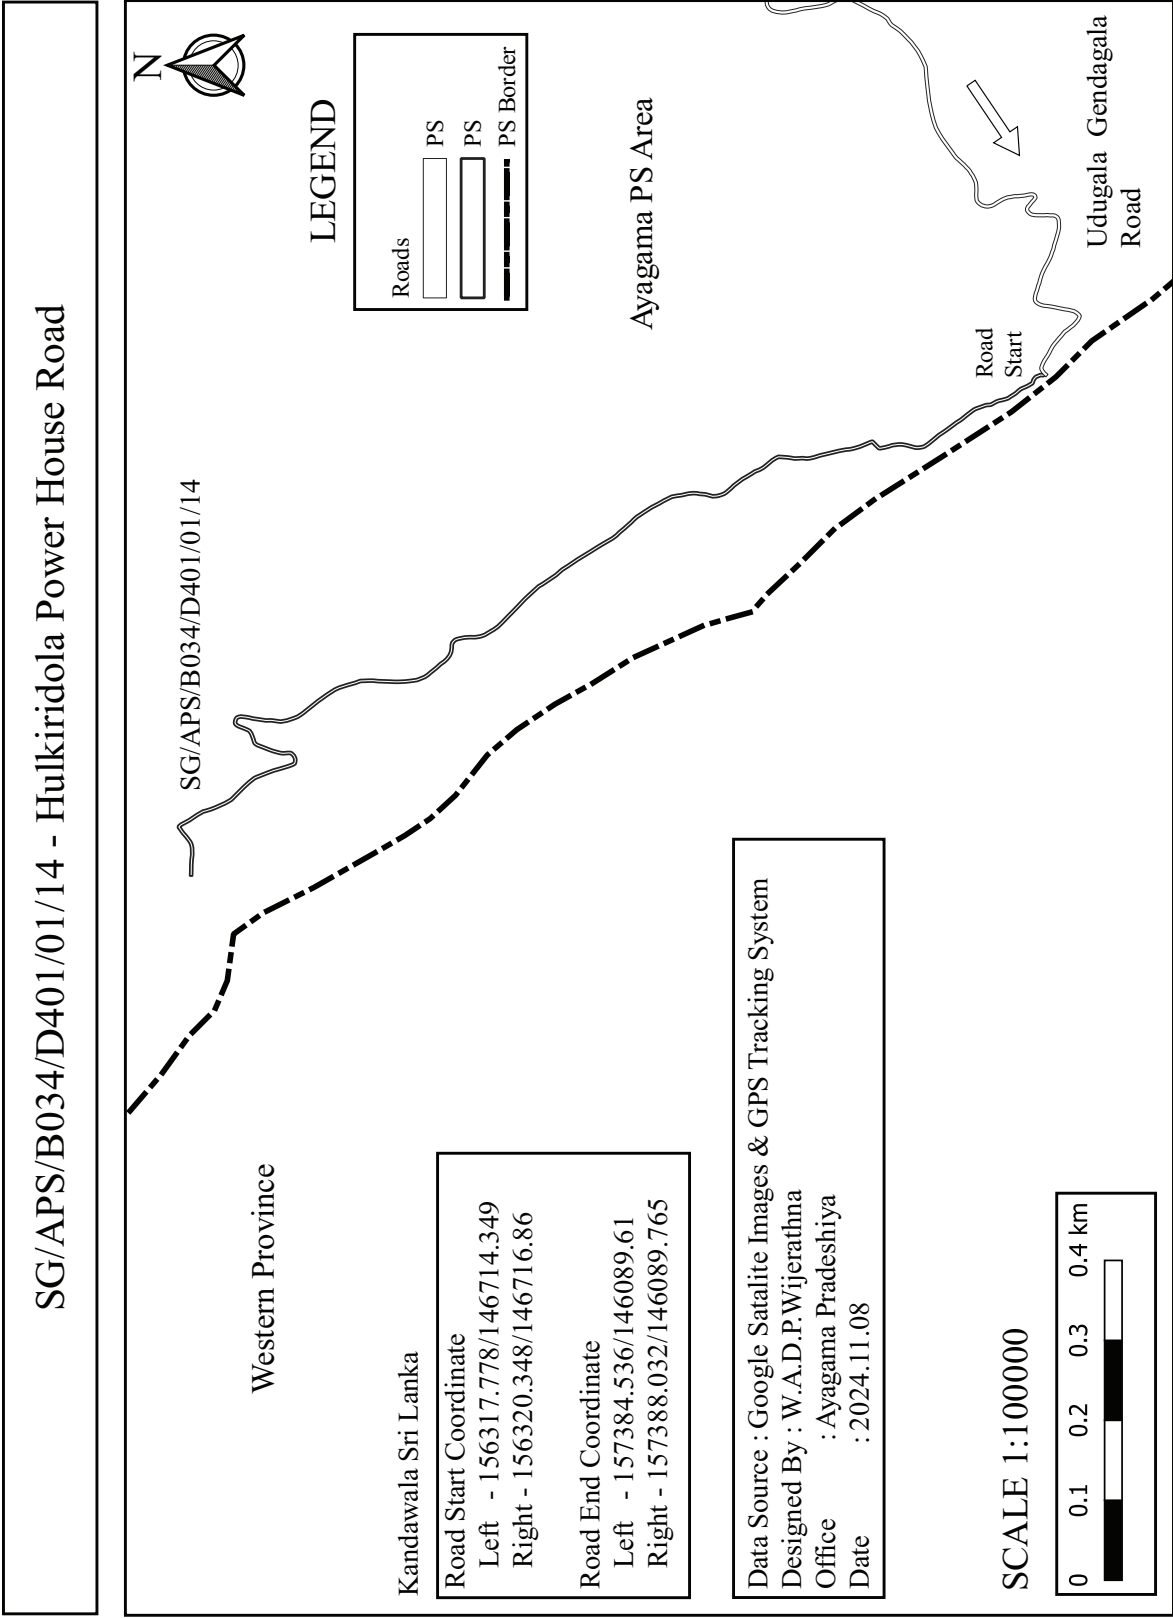


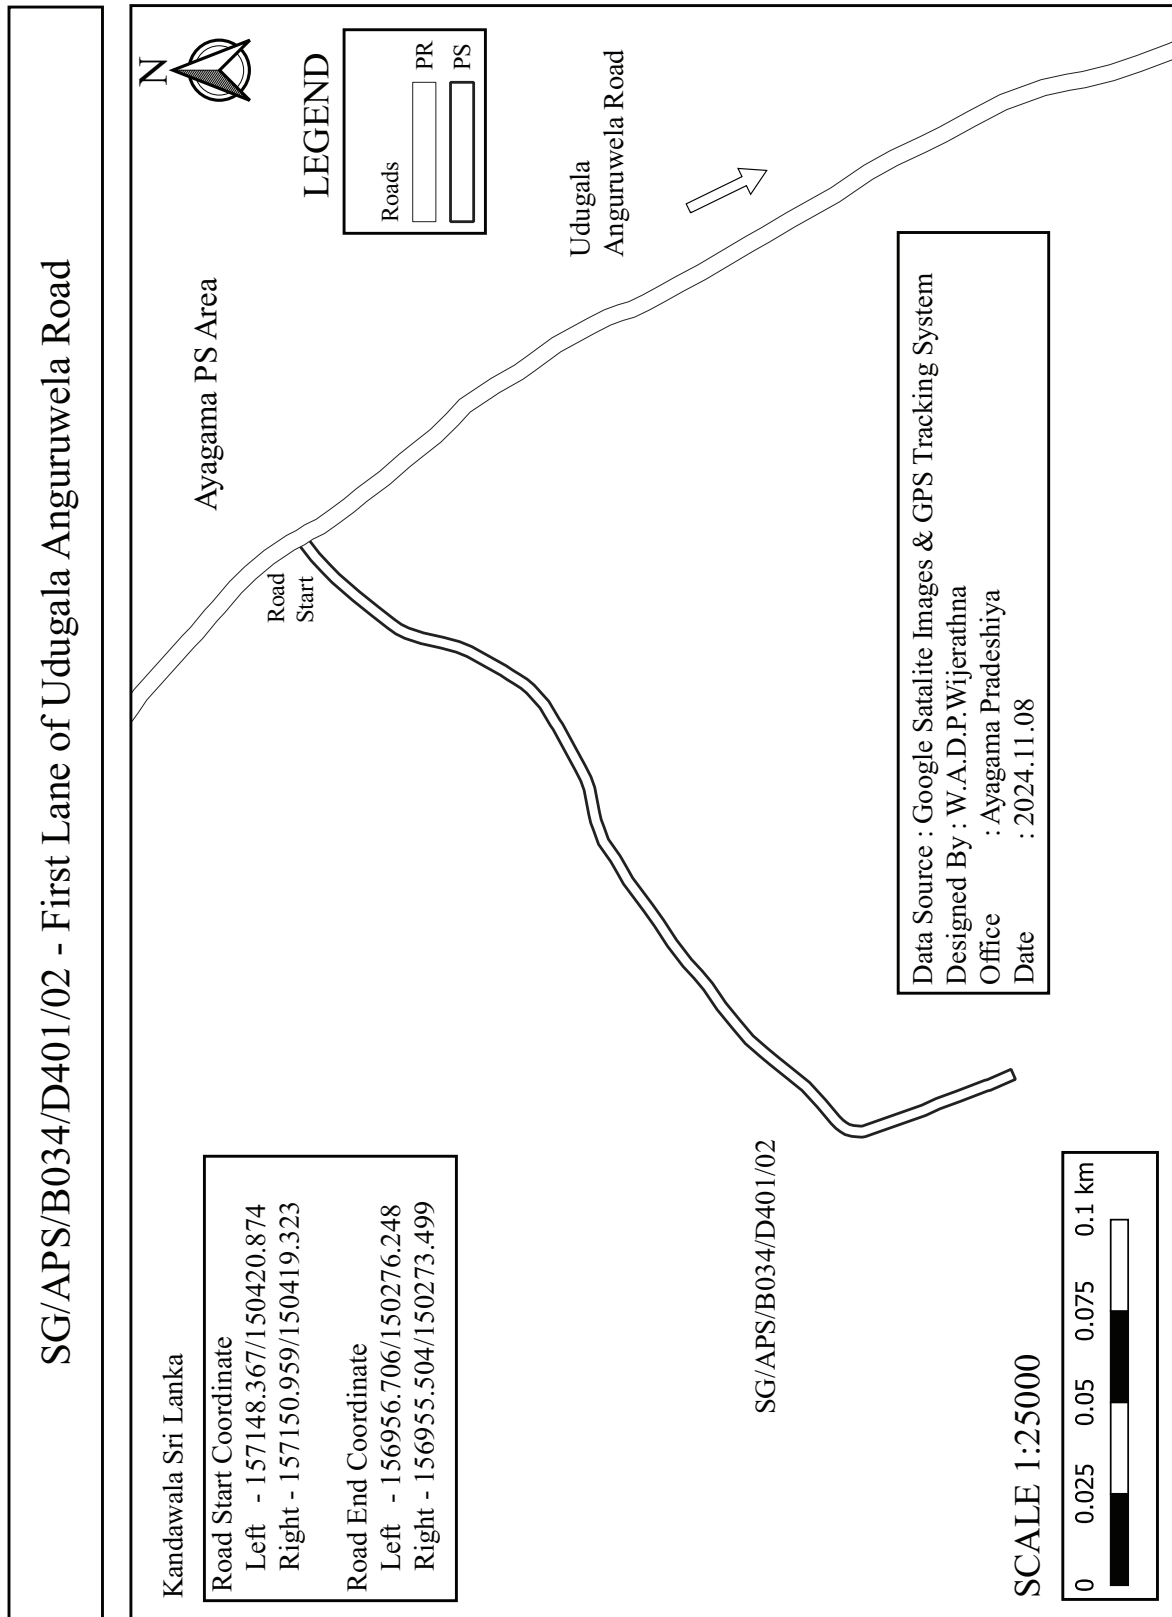


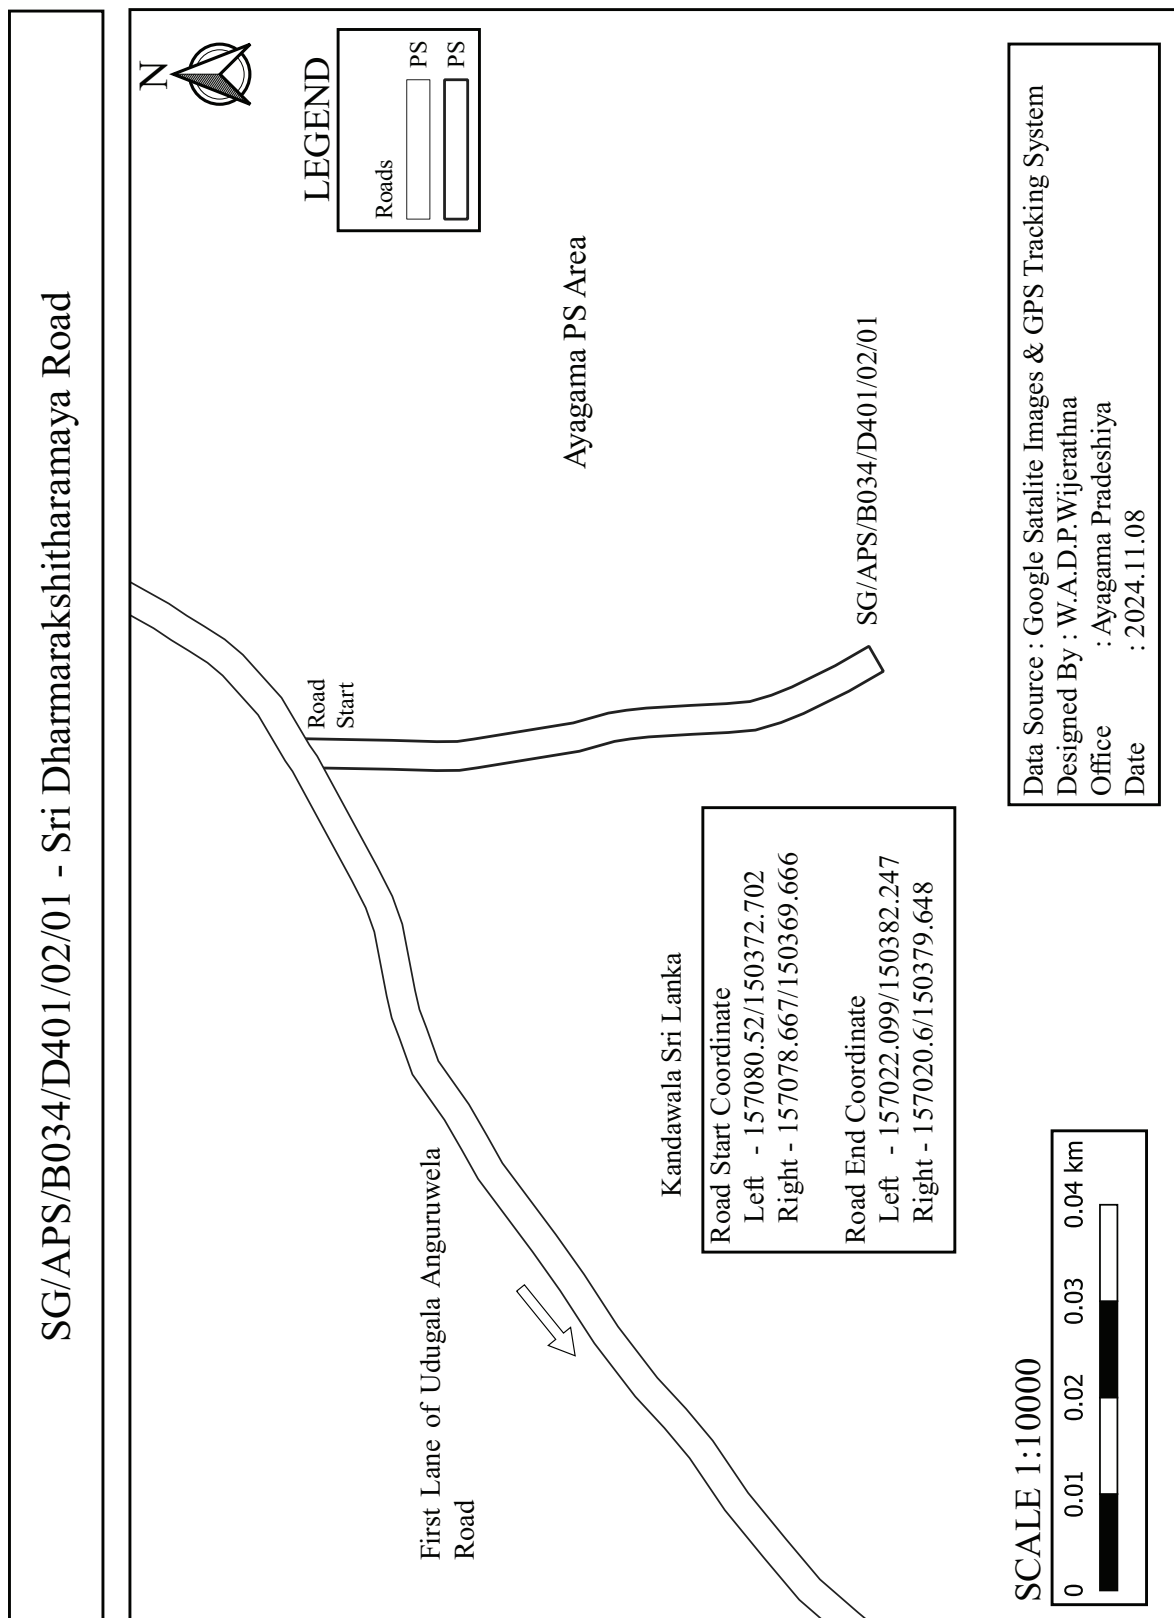


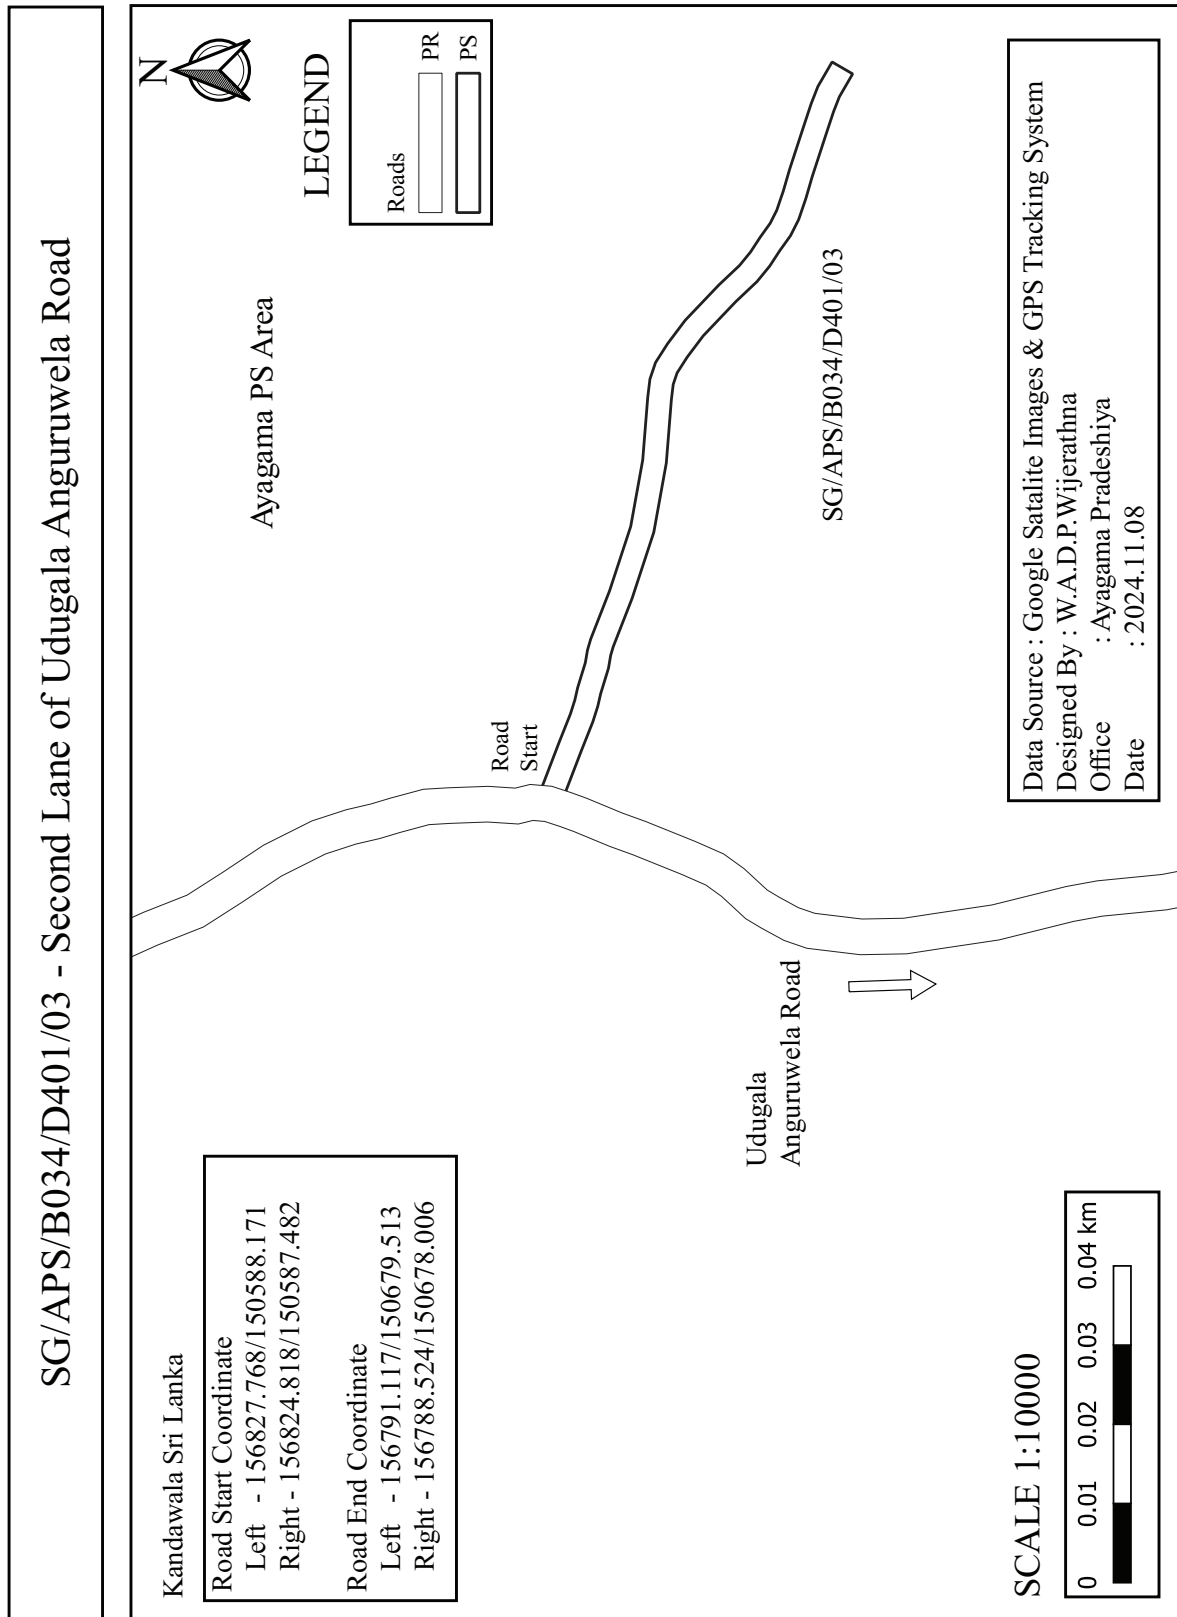


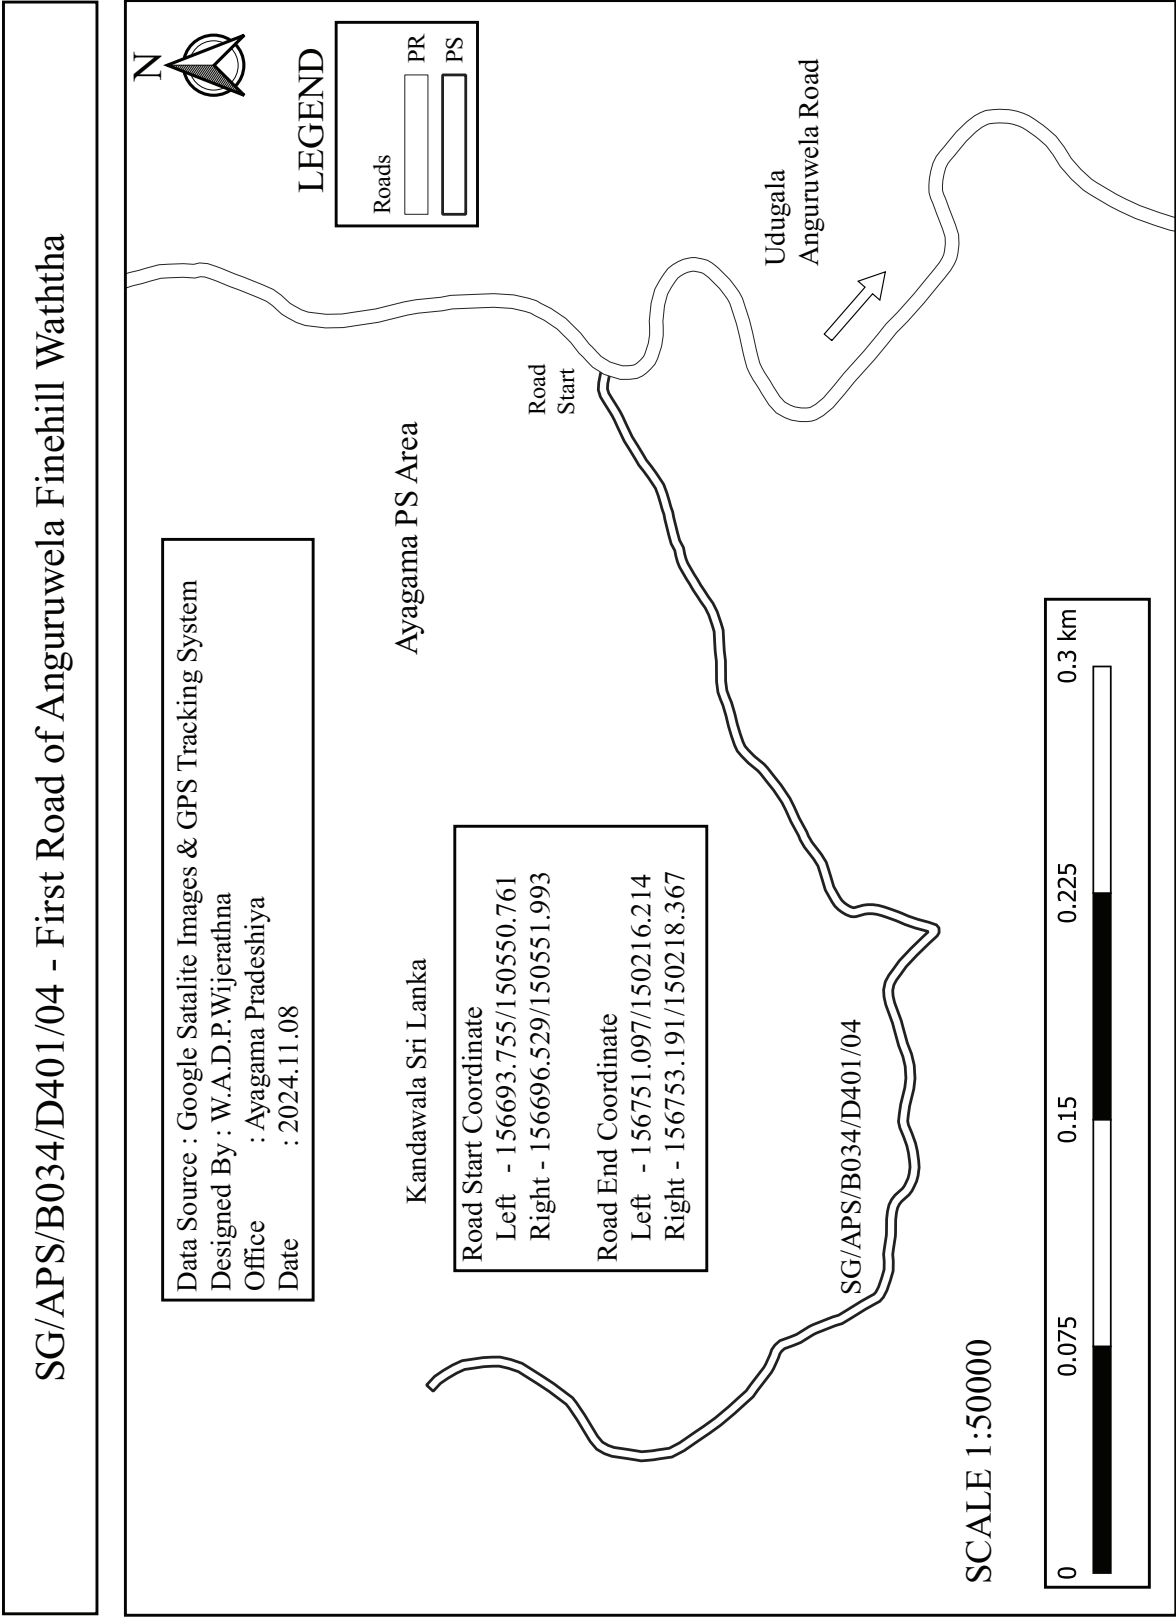


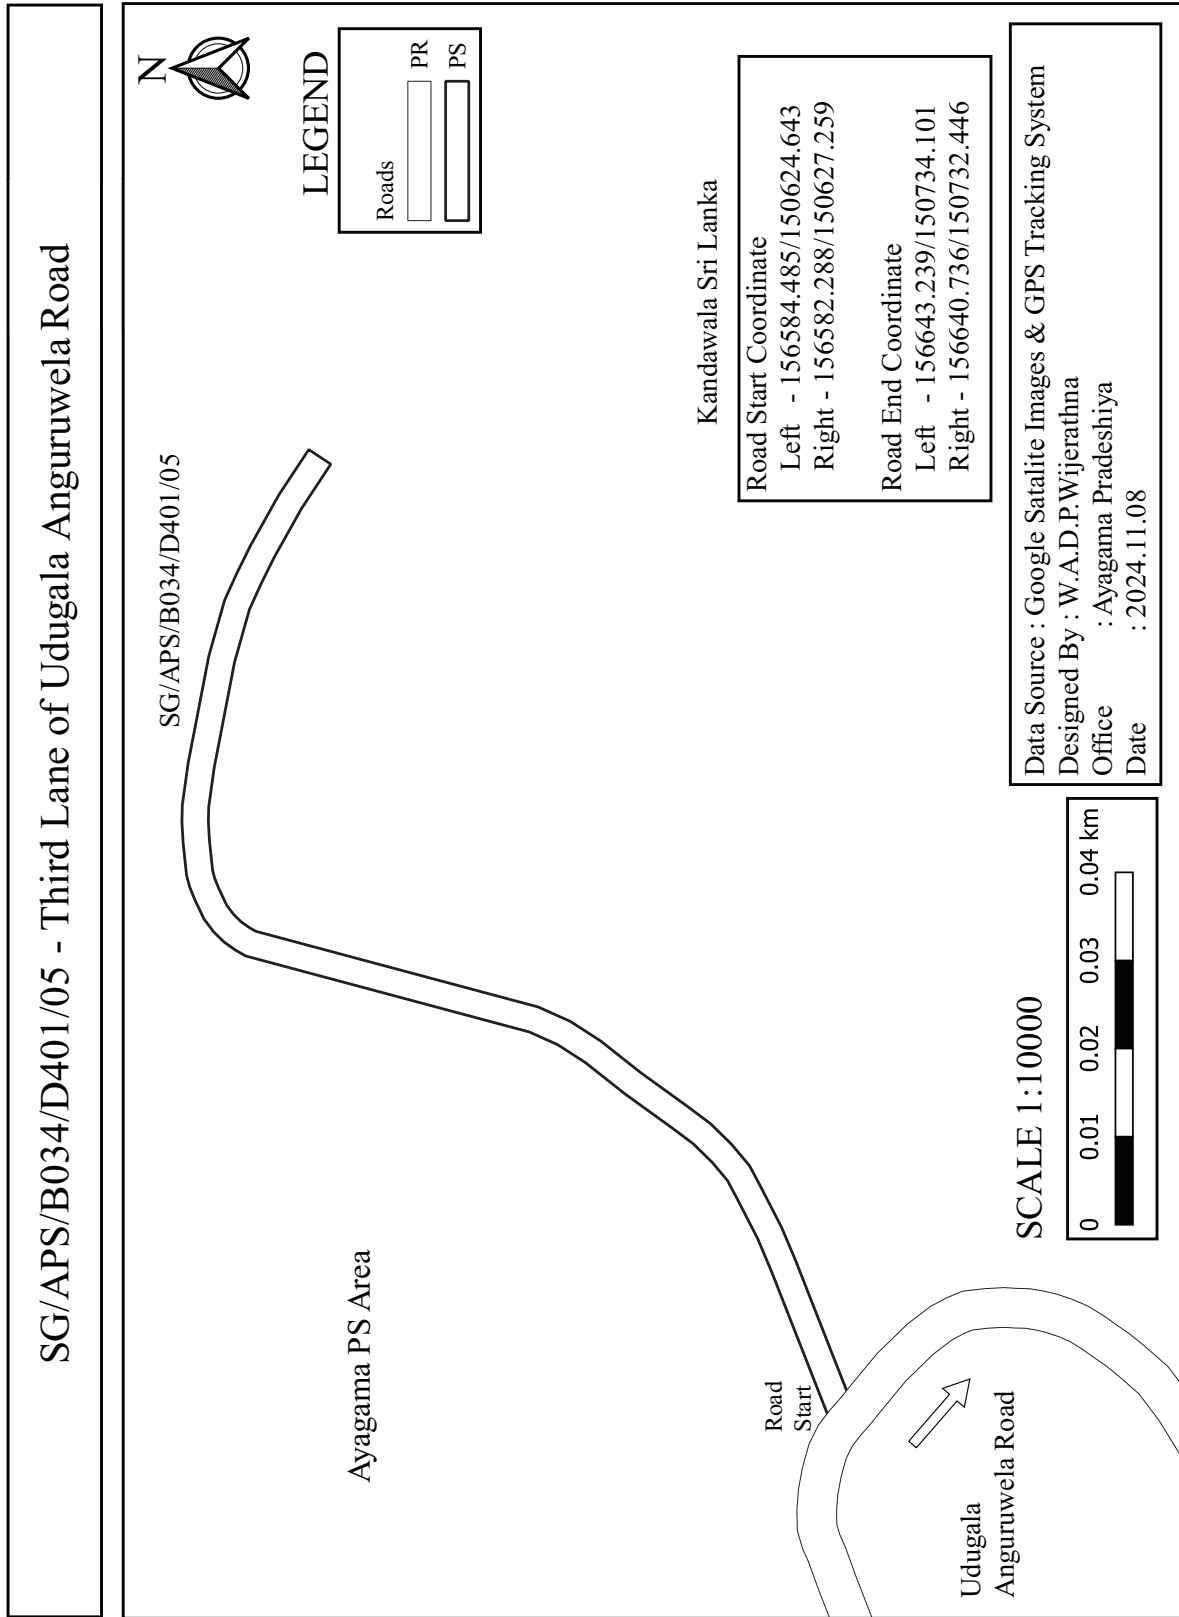


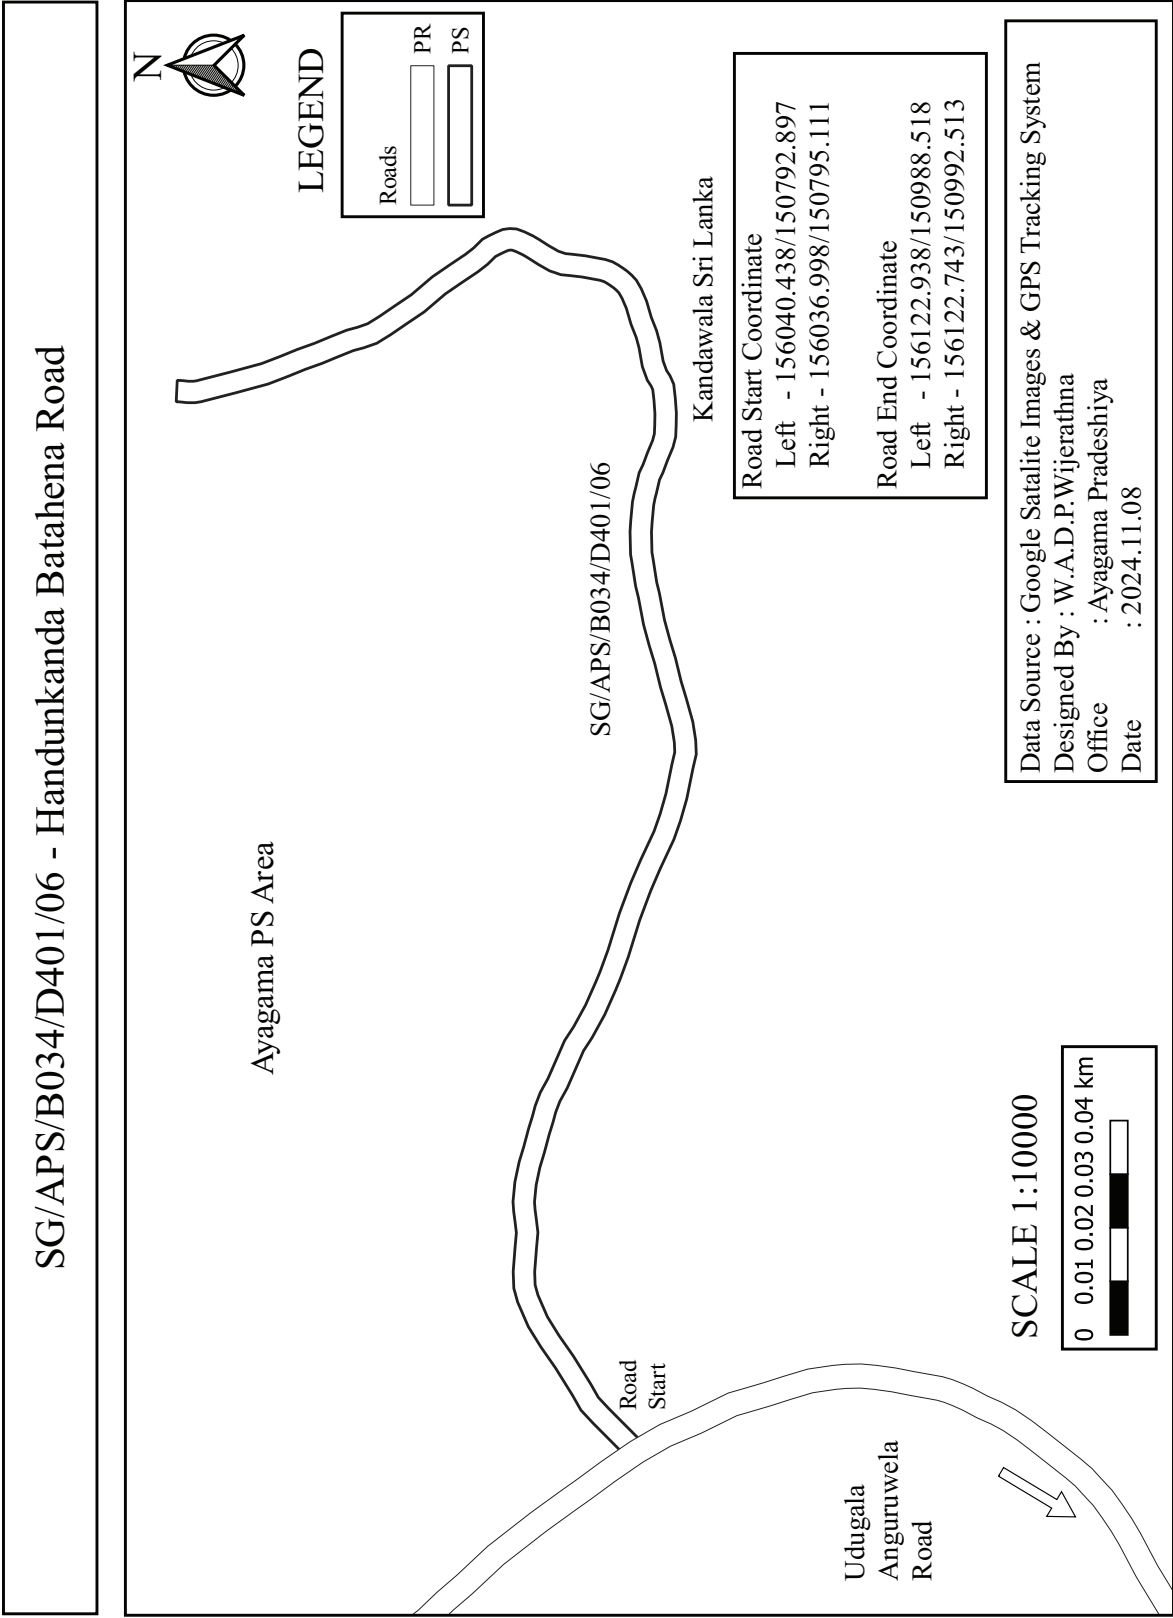


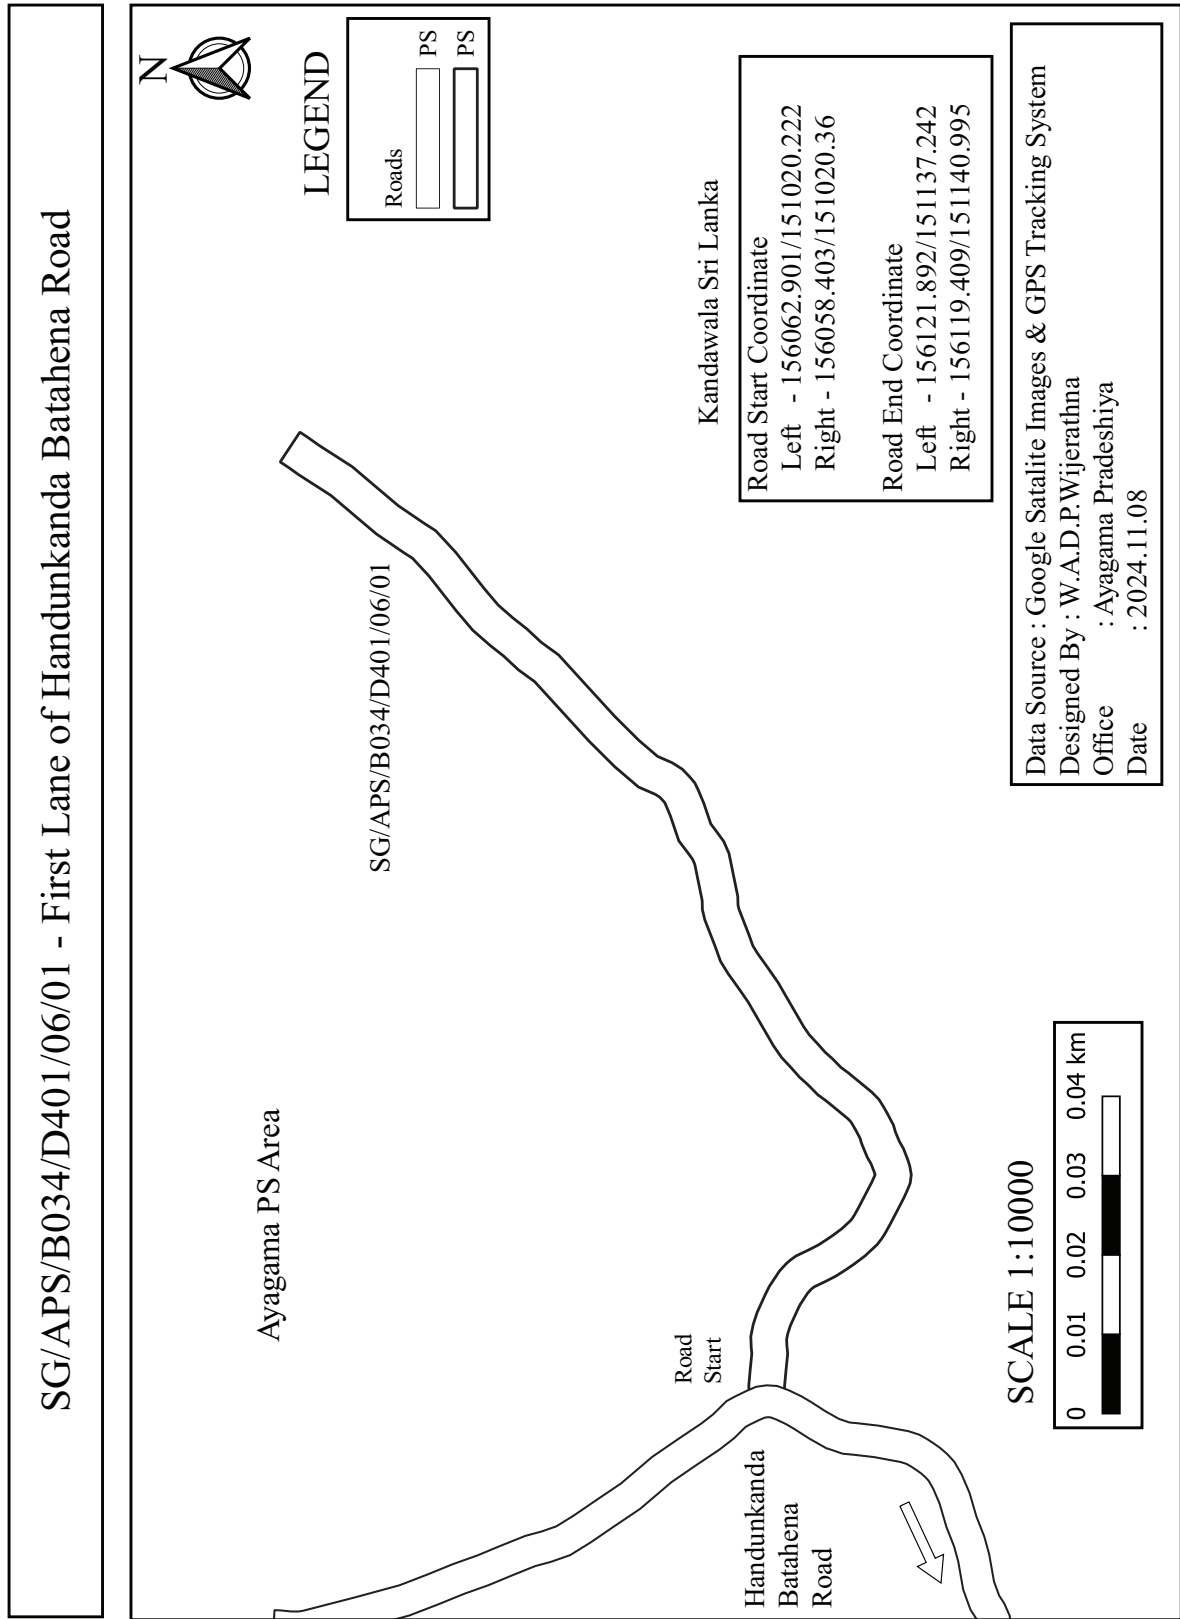


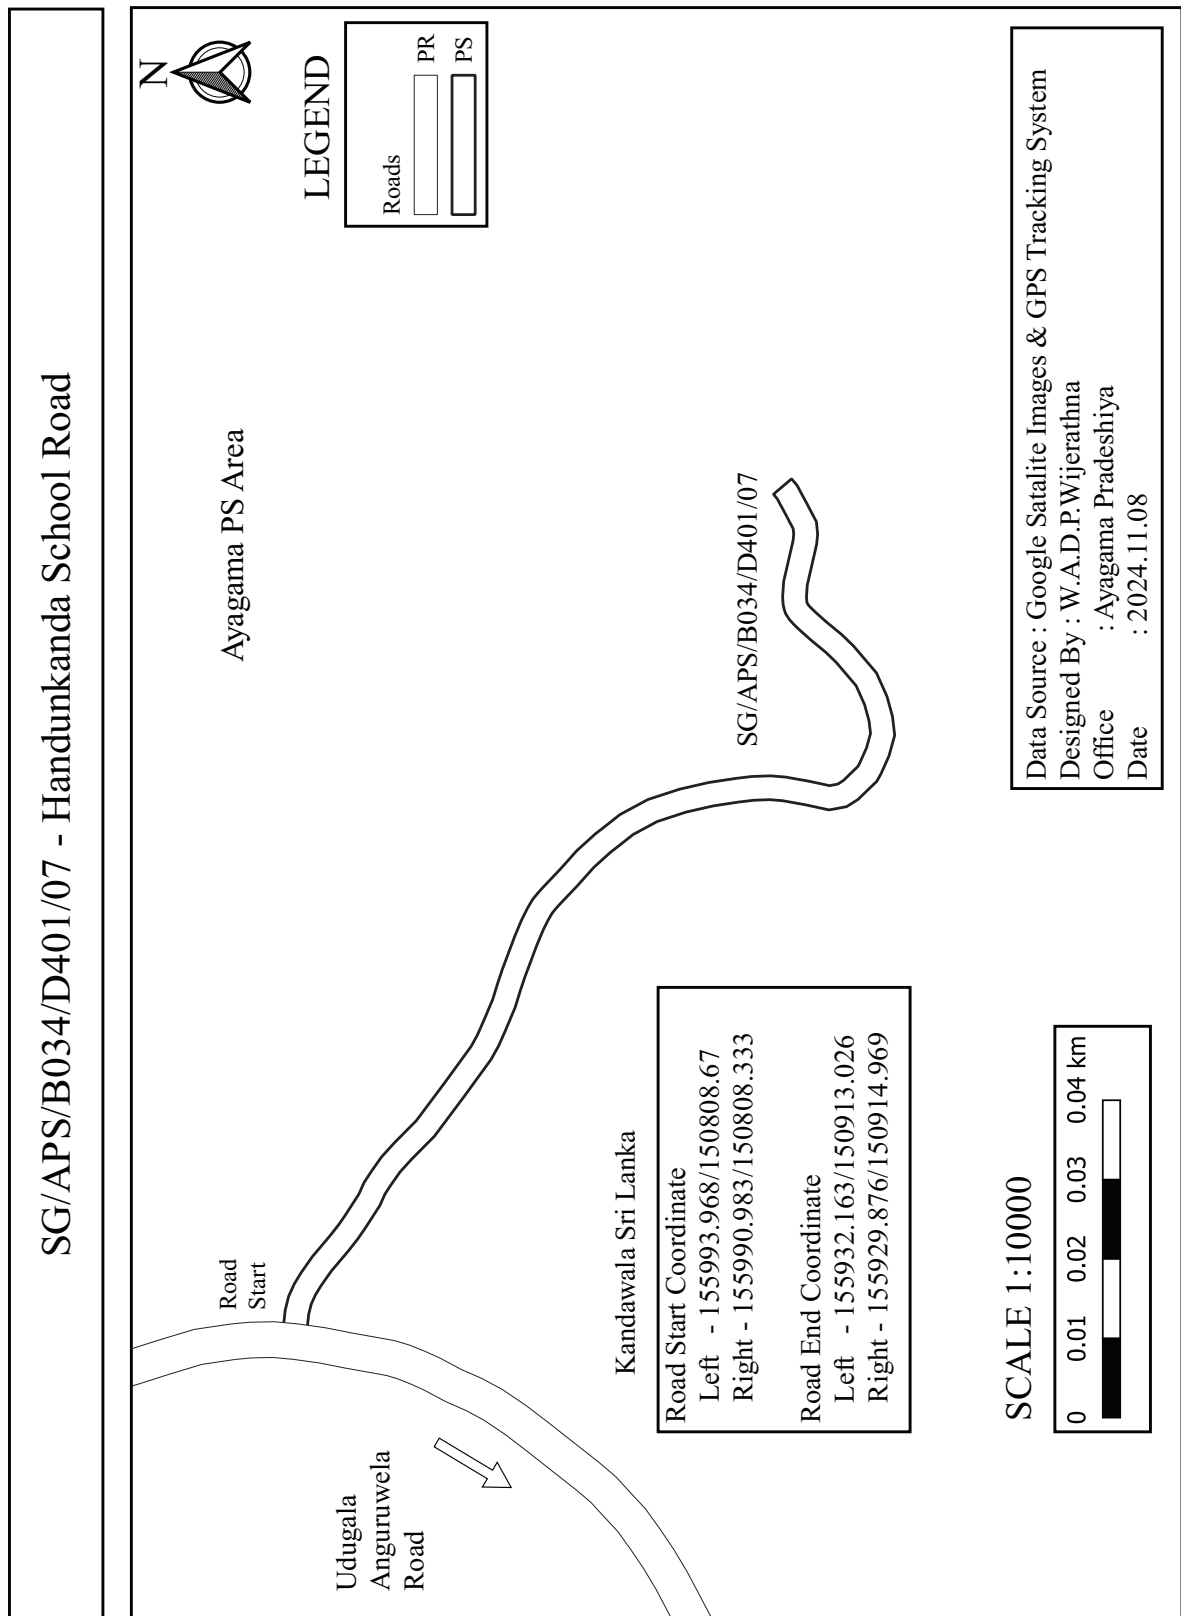

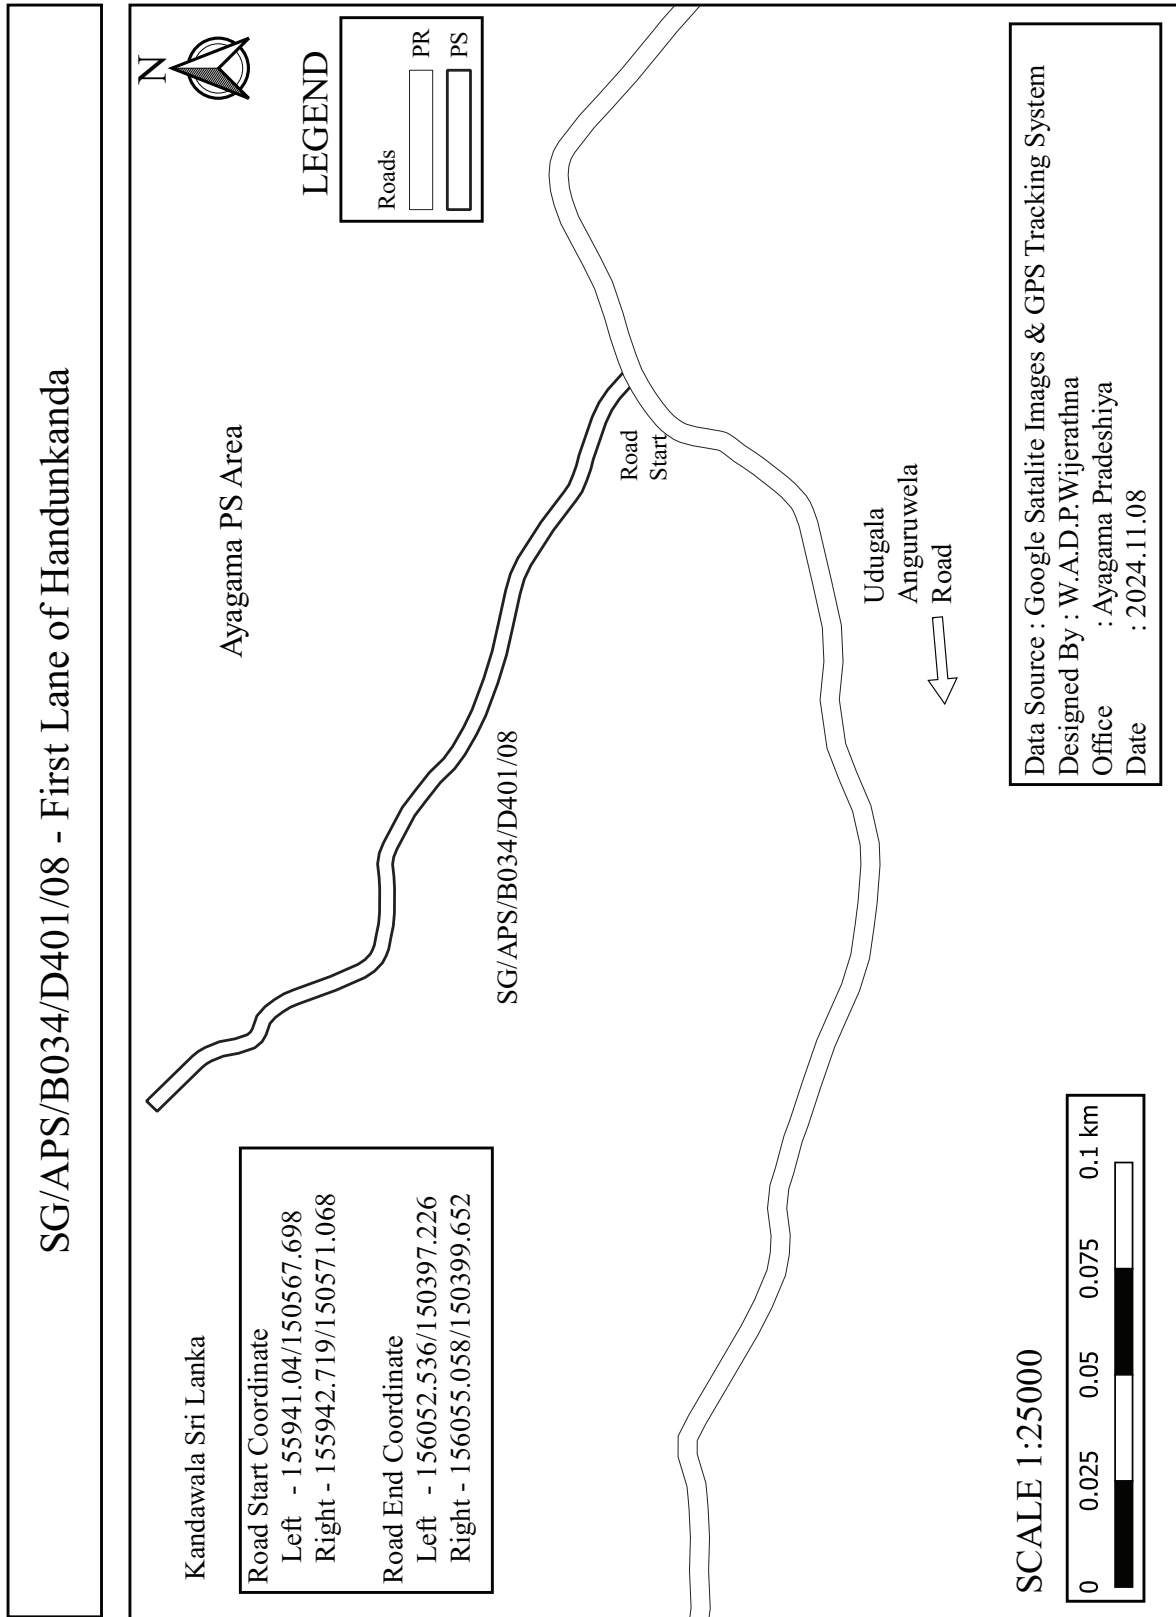


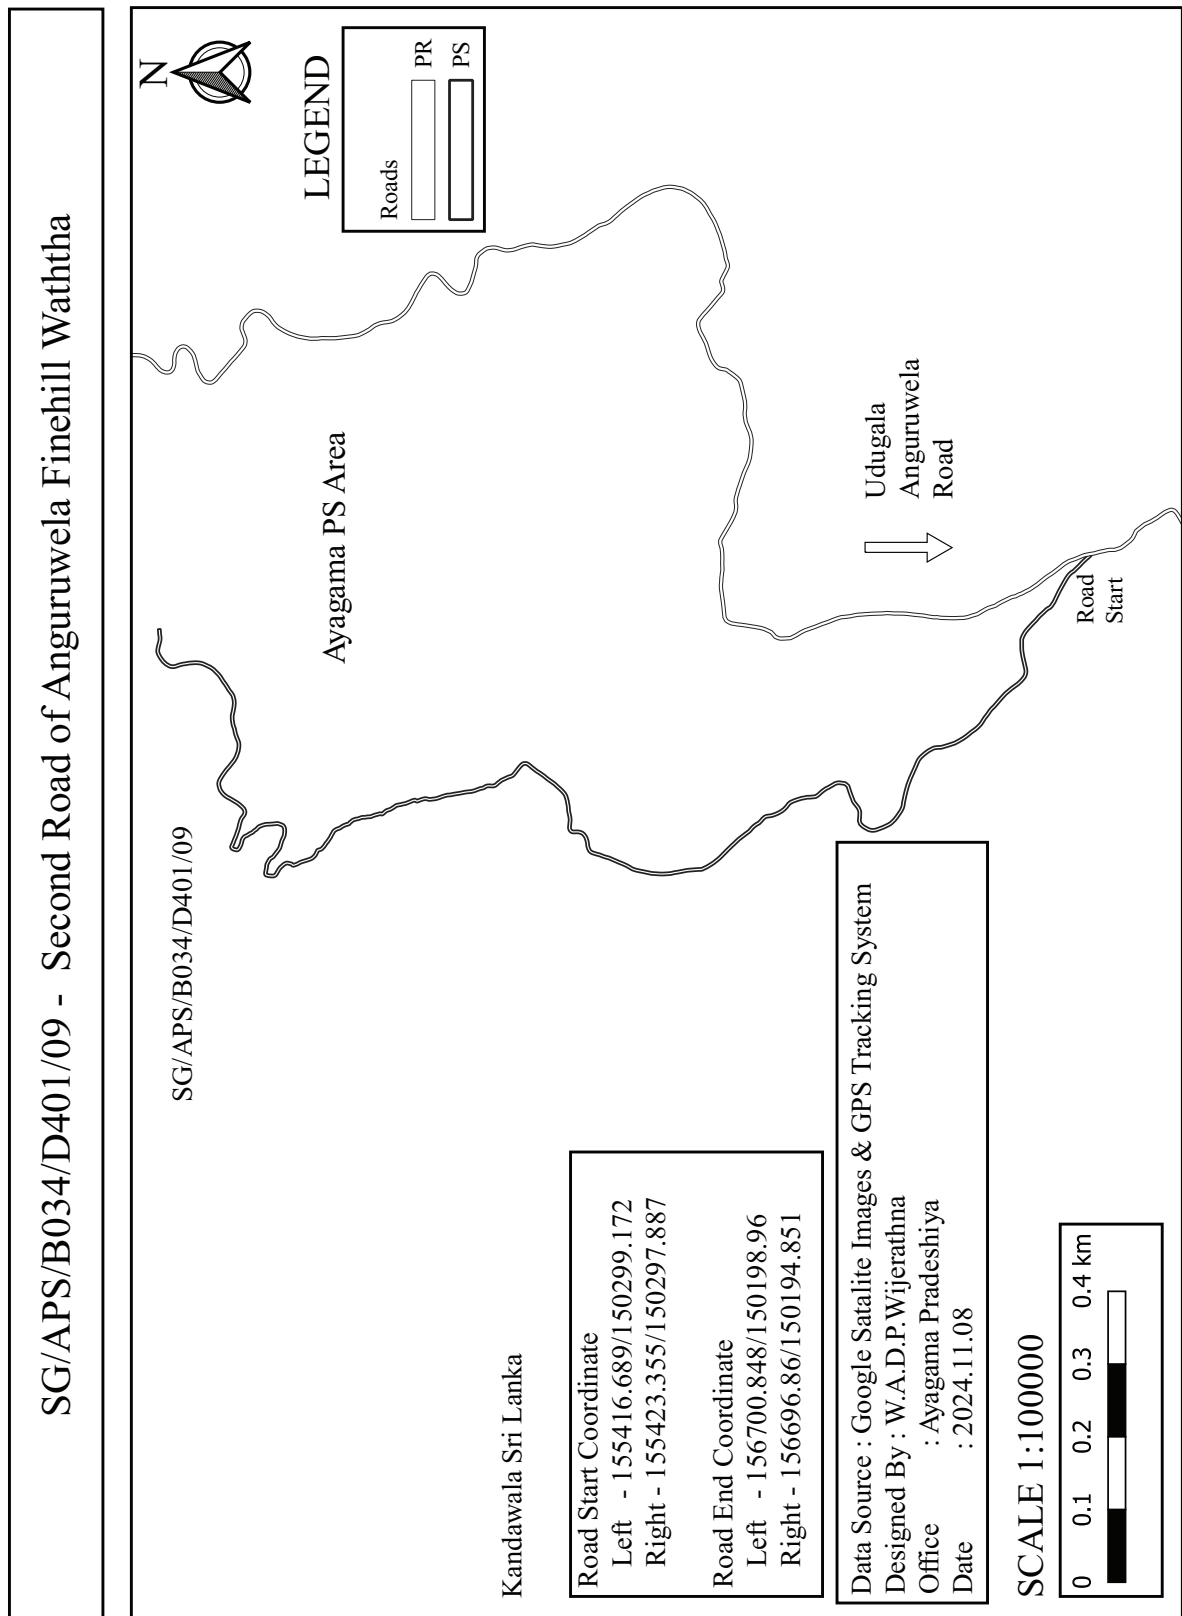


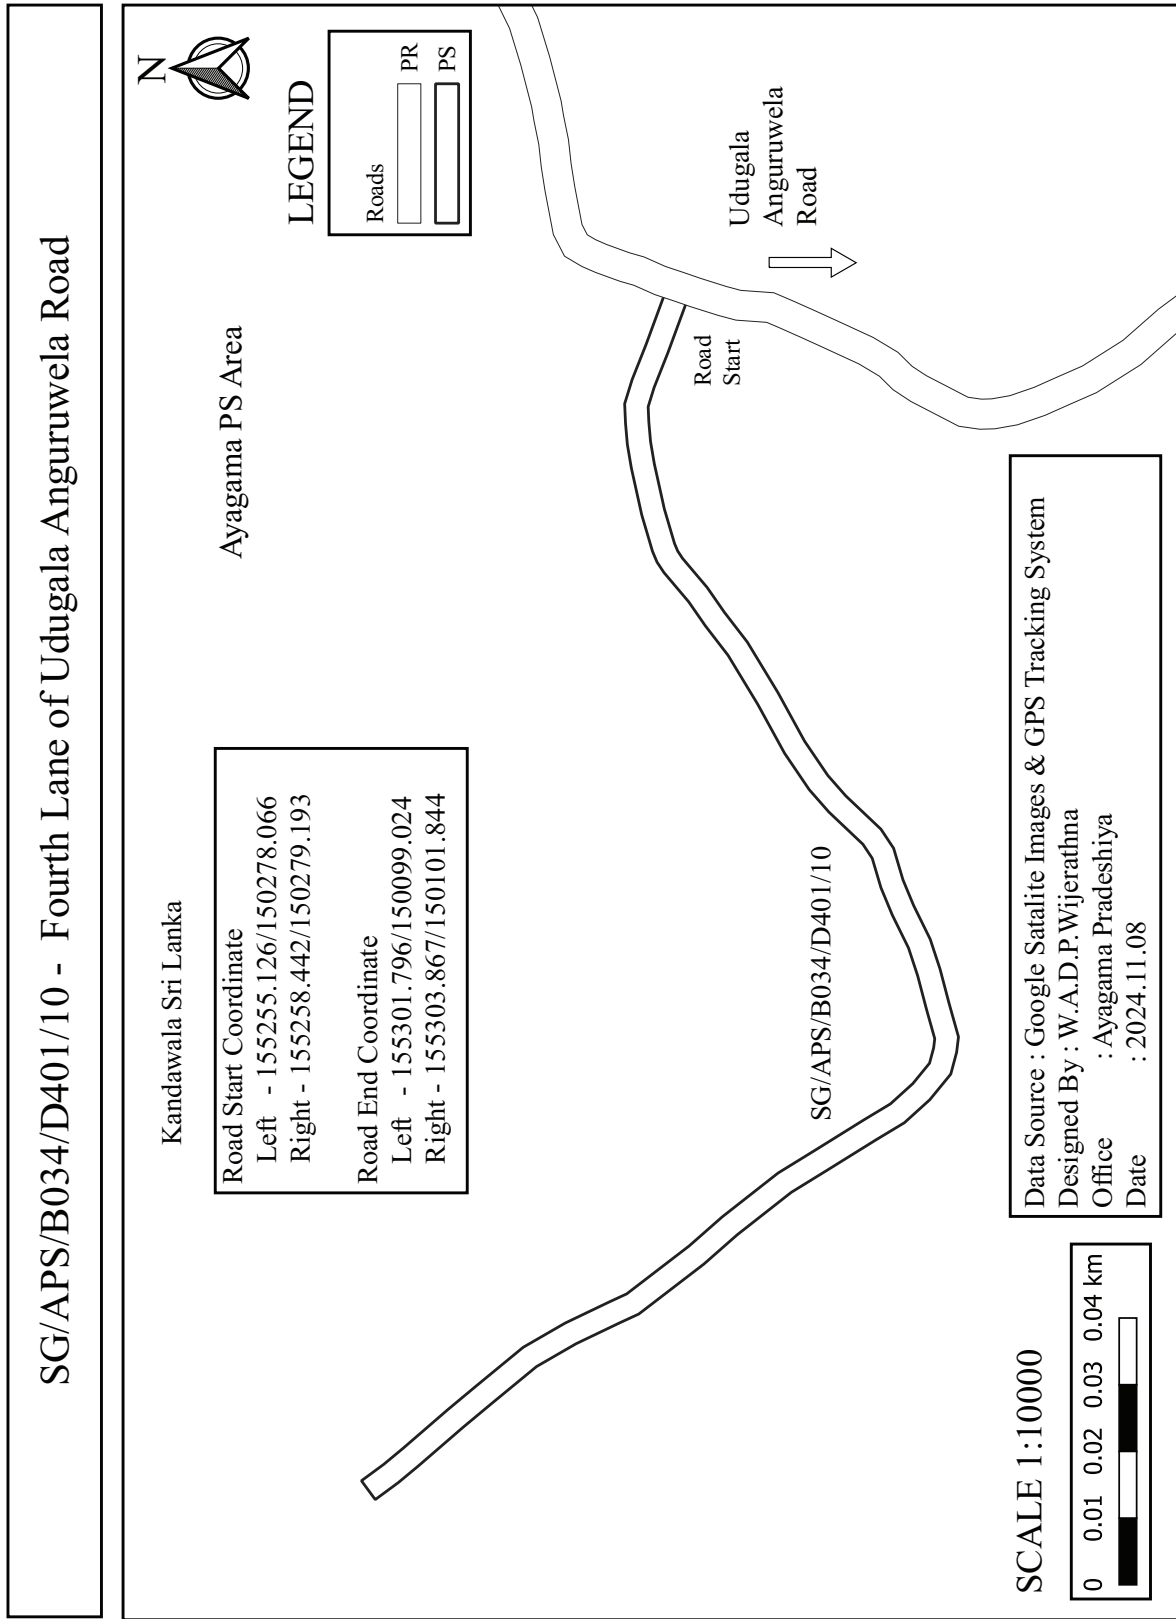


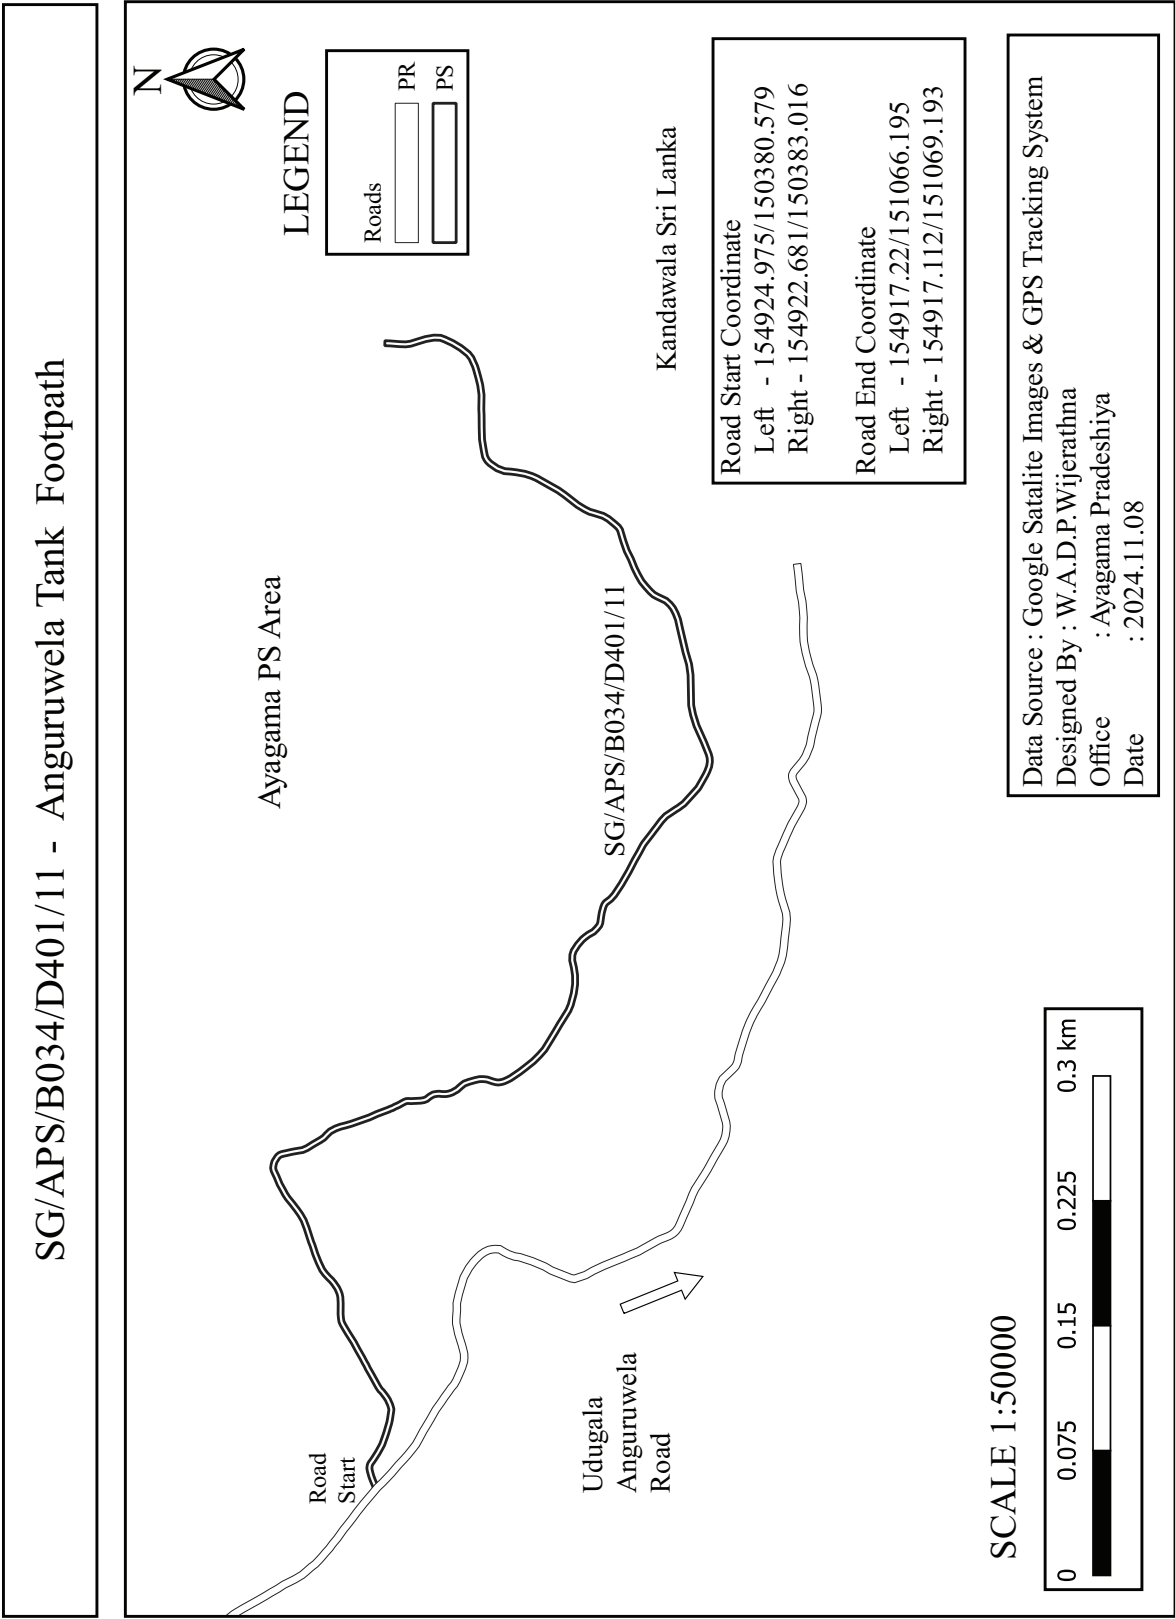


SG/APS/B034/D401/12 - First Lane of Panwilahena

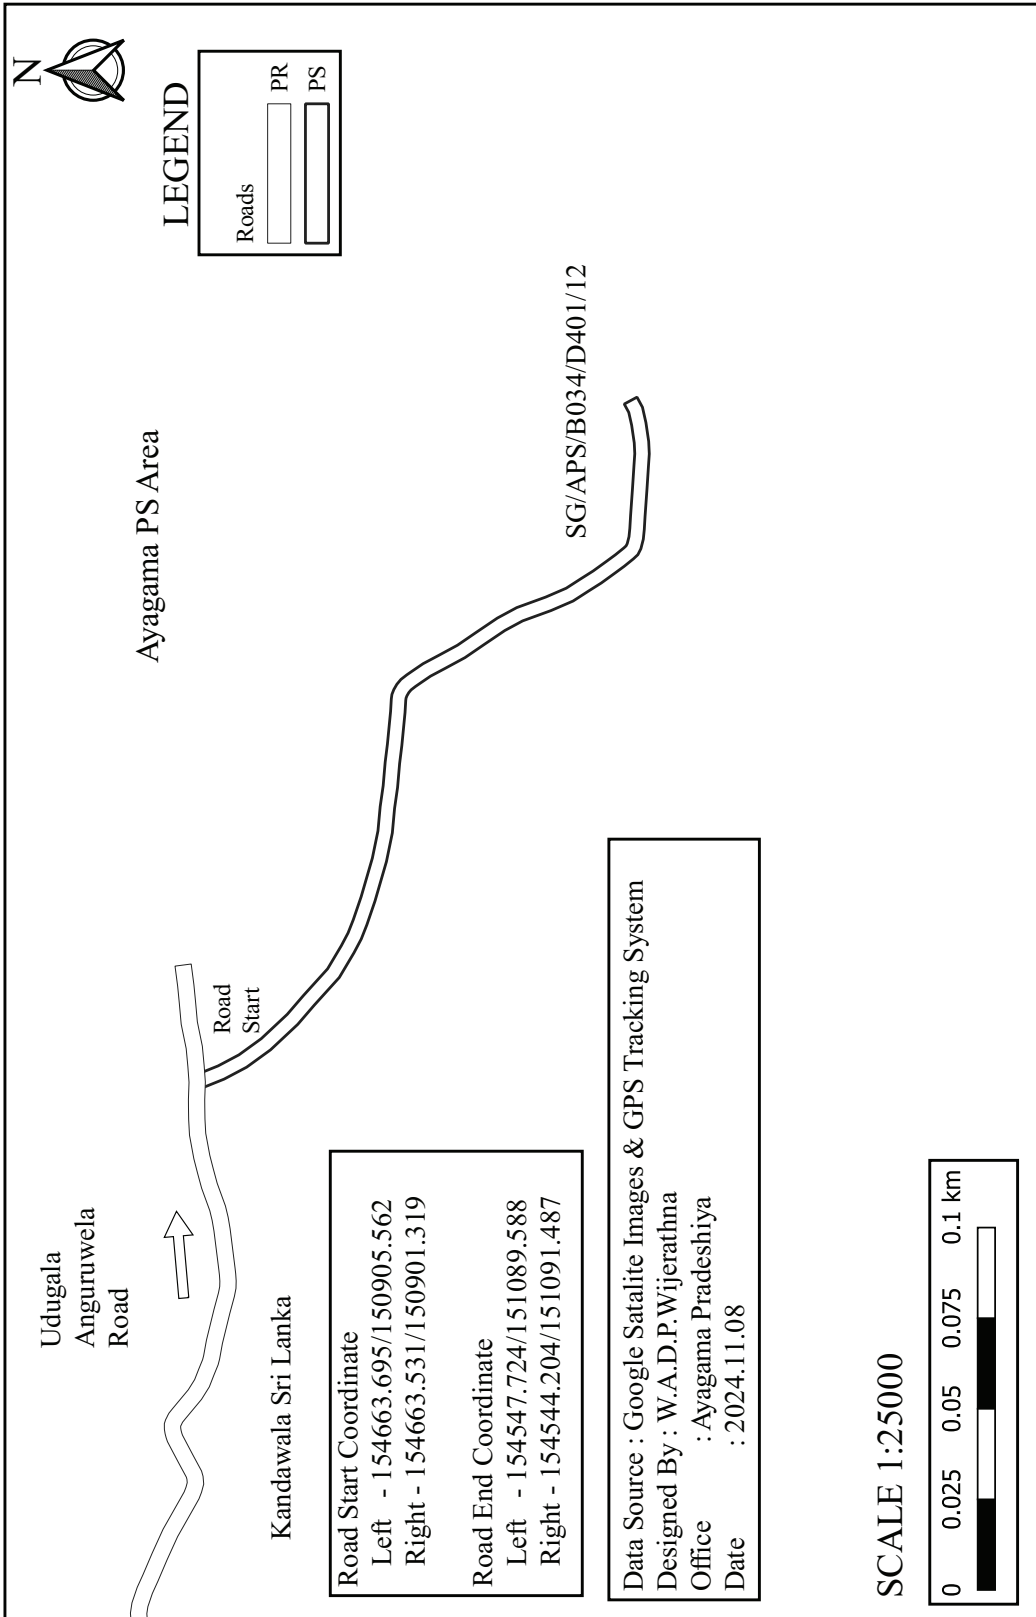

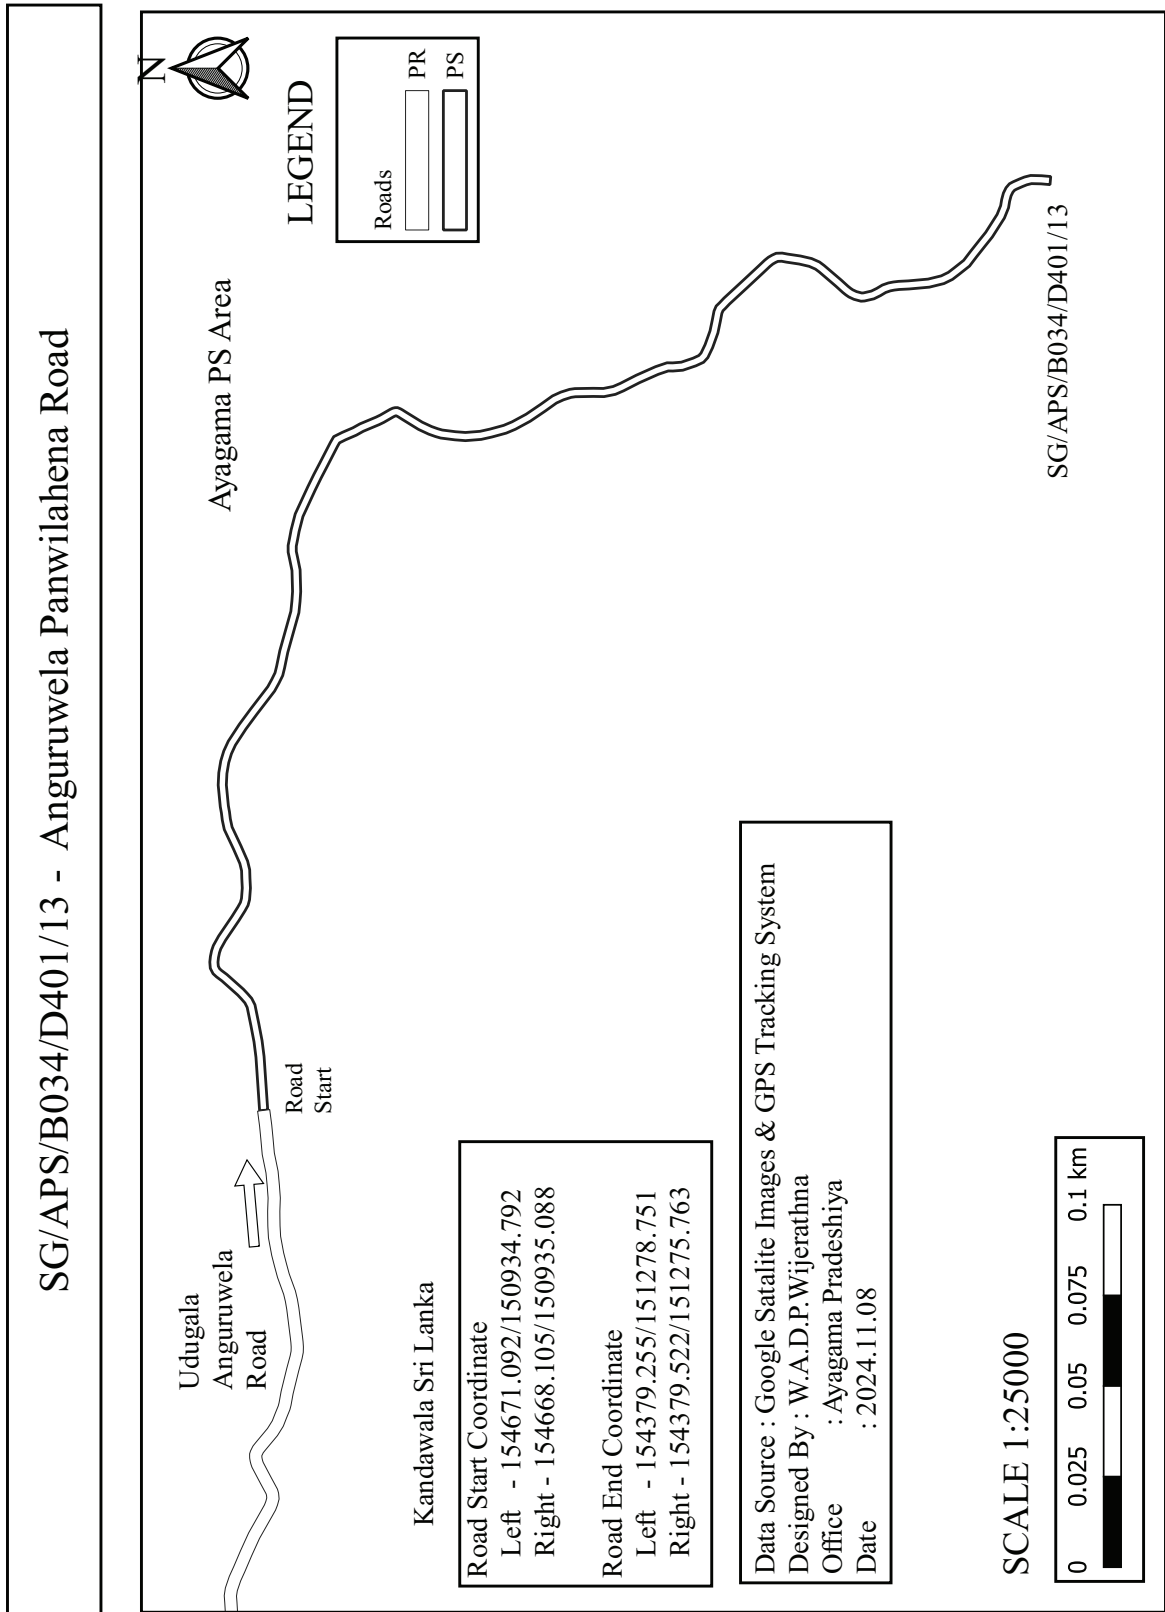

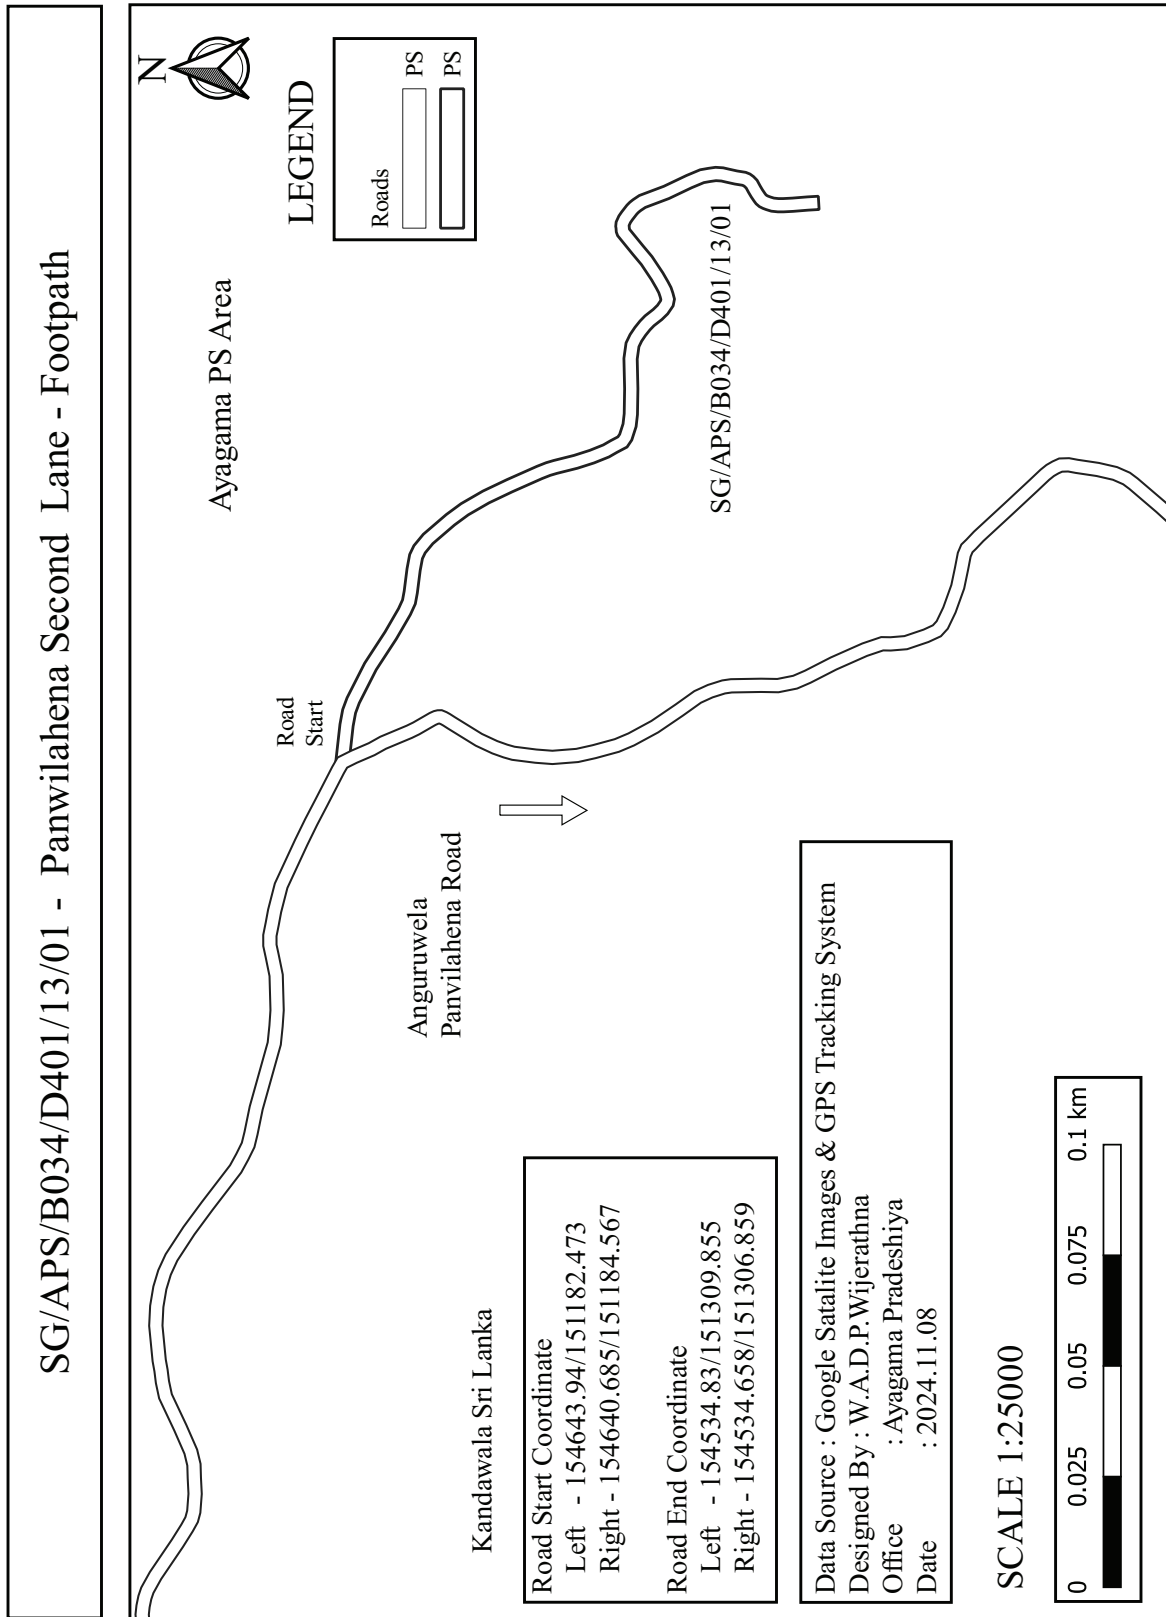

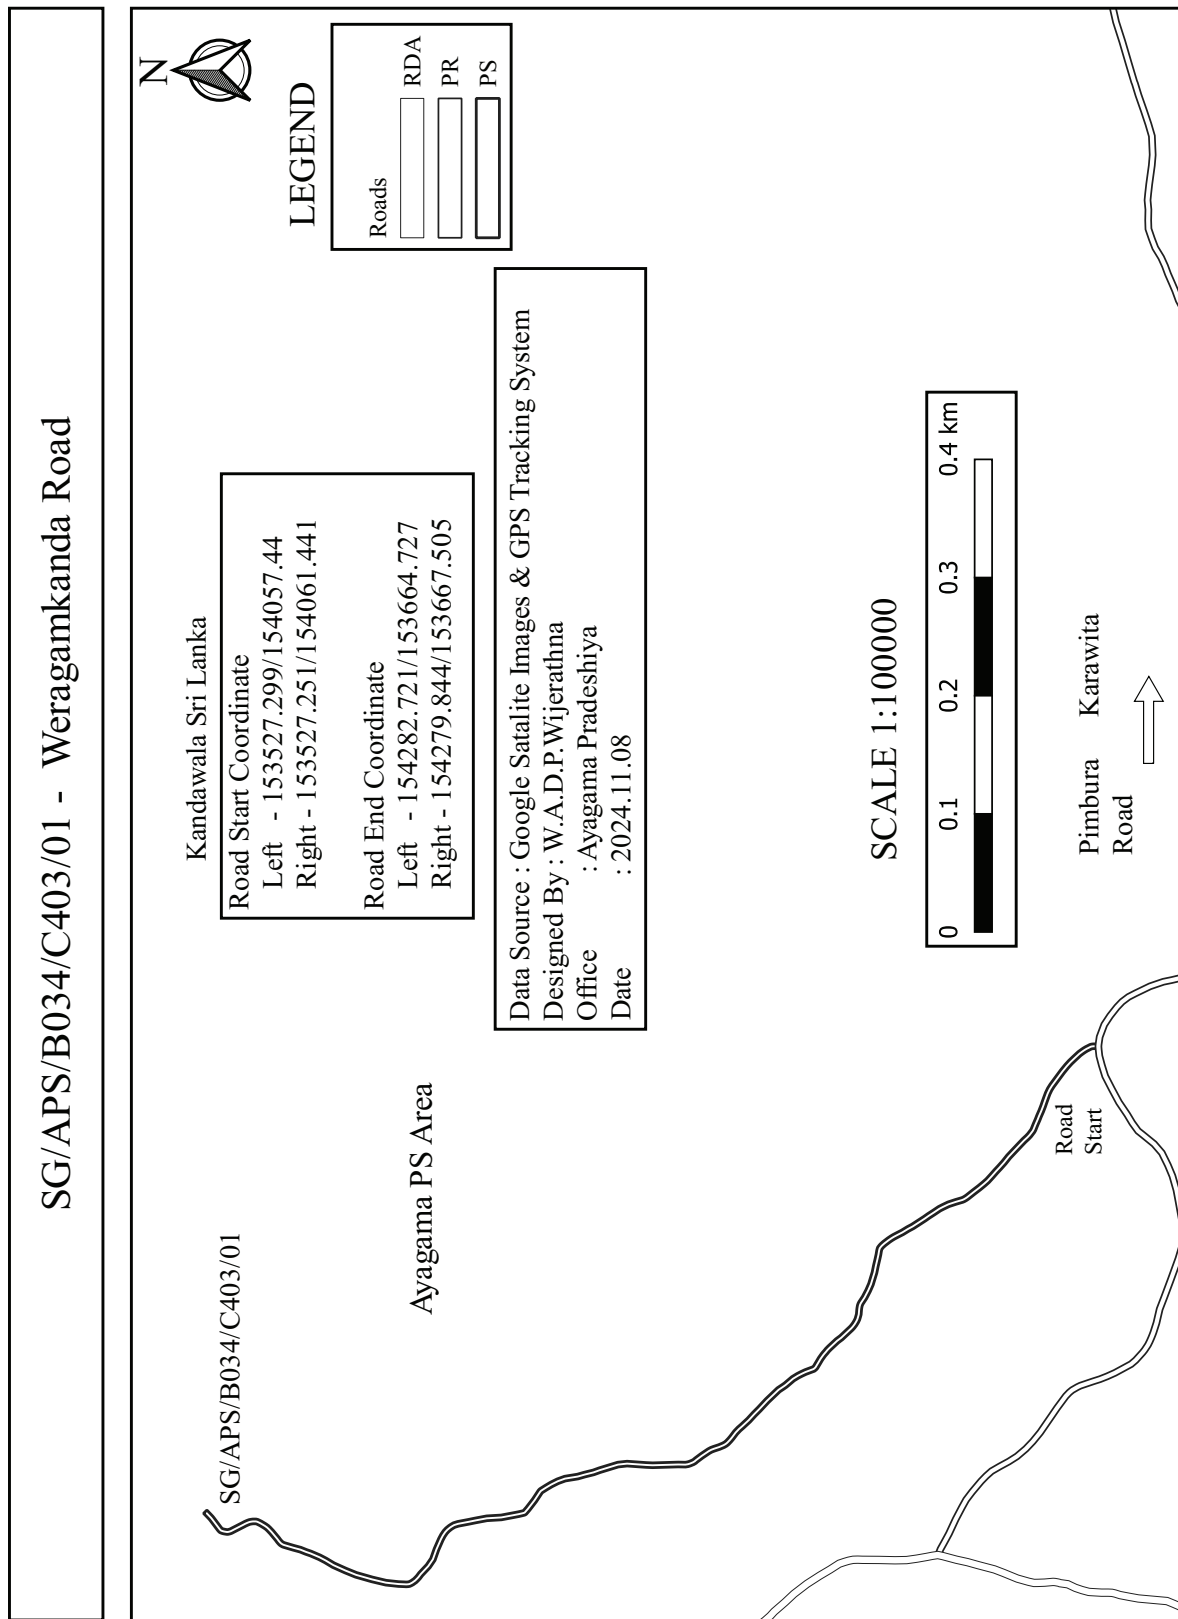

SG/APS/B034/C403/02 - Kukuluwa Rajamaha vihara First Mawatha

Data Source : Google Satalite Images & GPS Tracking System
Designed By : W.A.D.P.Wijerathna
Office : Ayagama Pradeshiya
Date : 2024.11.08

Kandawala Sri Lanka

Road Start Coordinate


Left - 153415.092/154520.334


Right - 153416.359/154526.083


Road End Coordinate

Left - 154548.876/155593.224


Right - 154549.724/155596.62

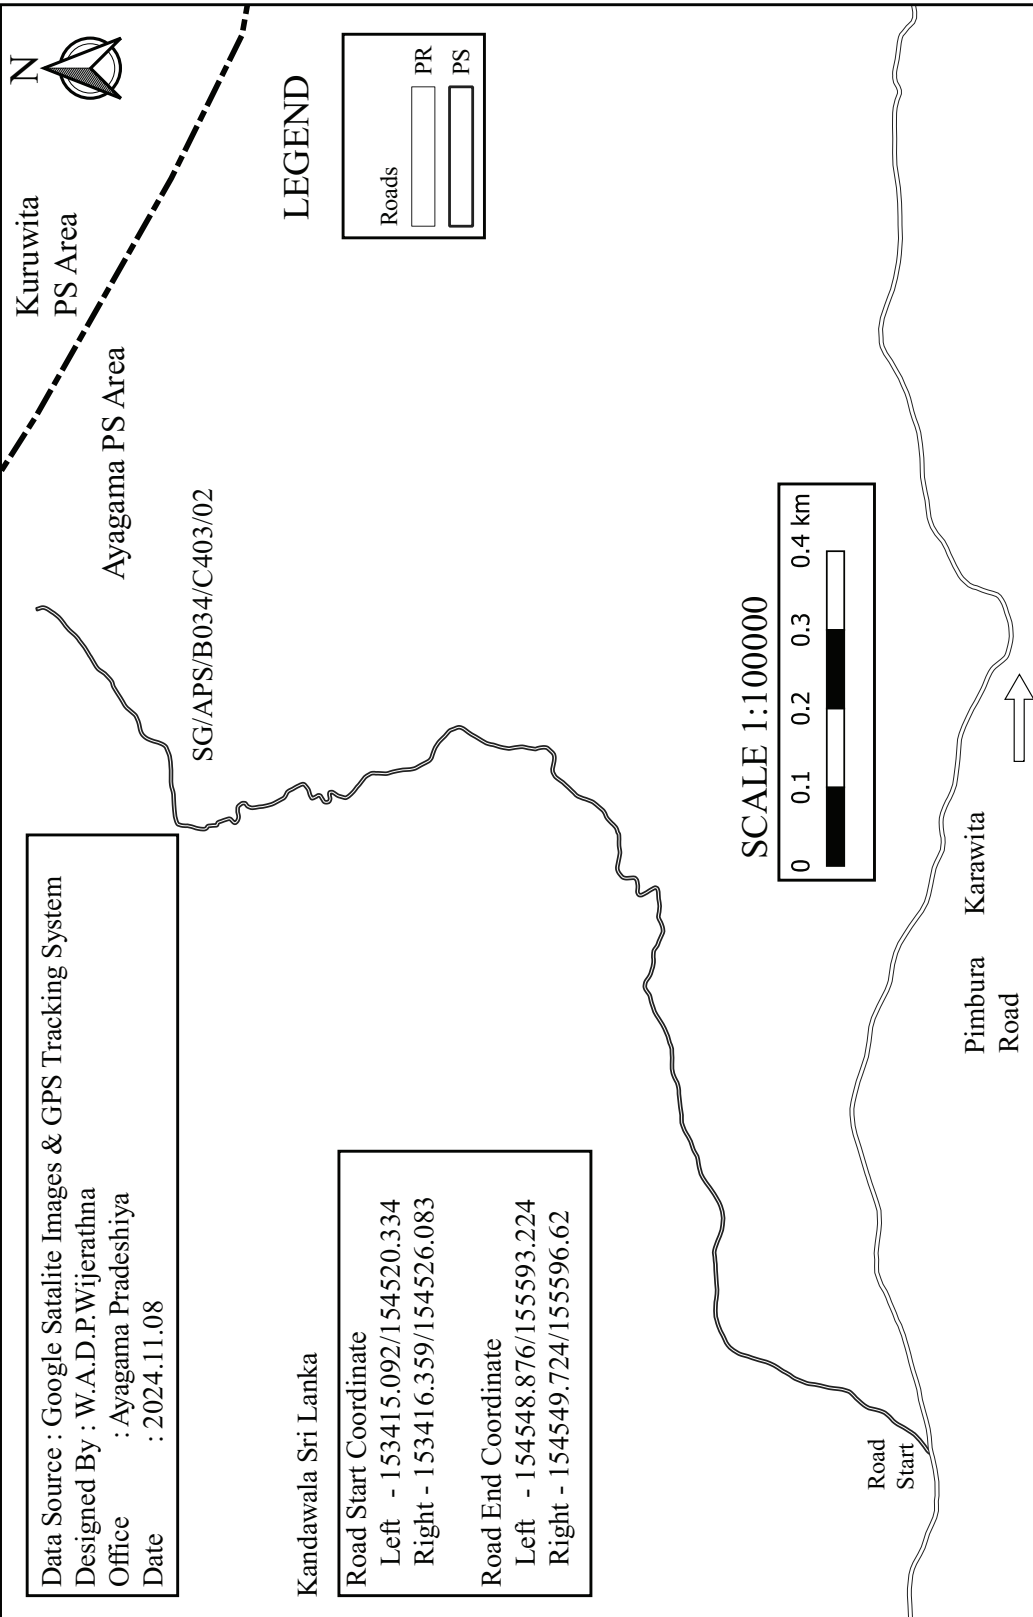


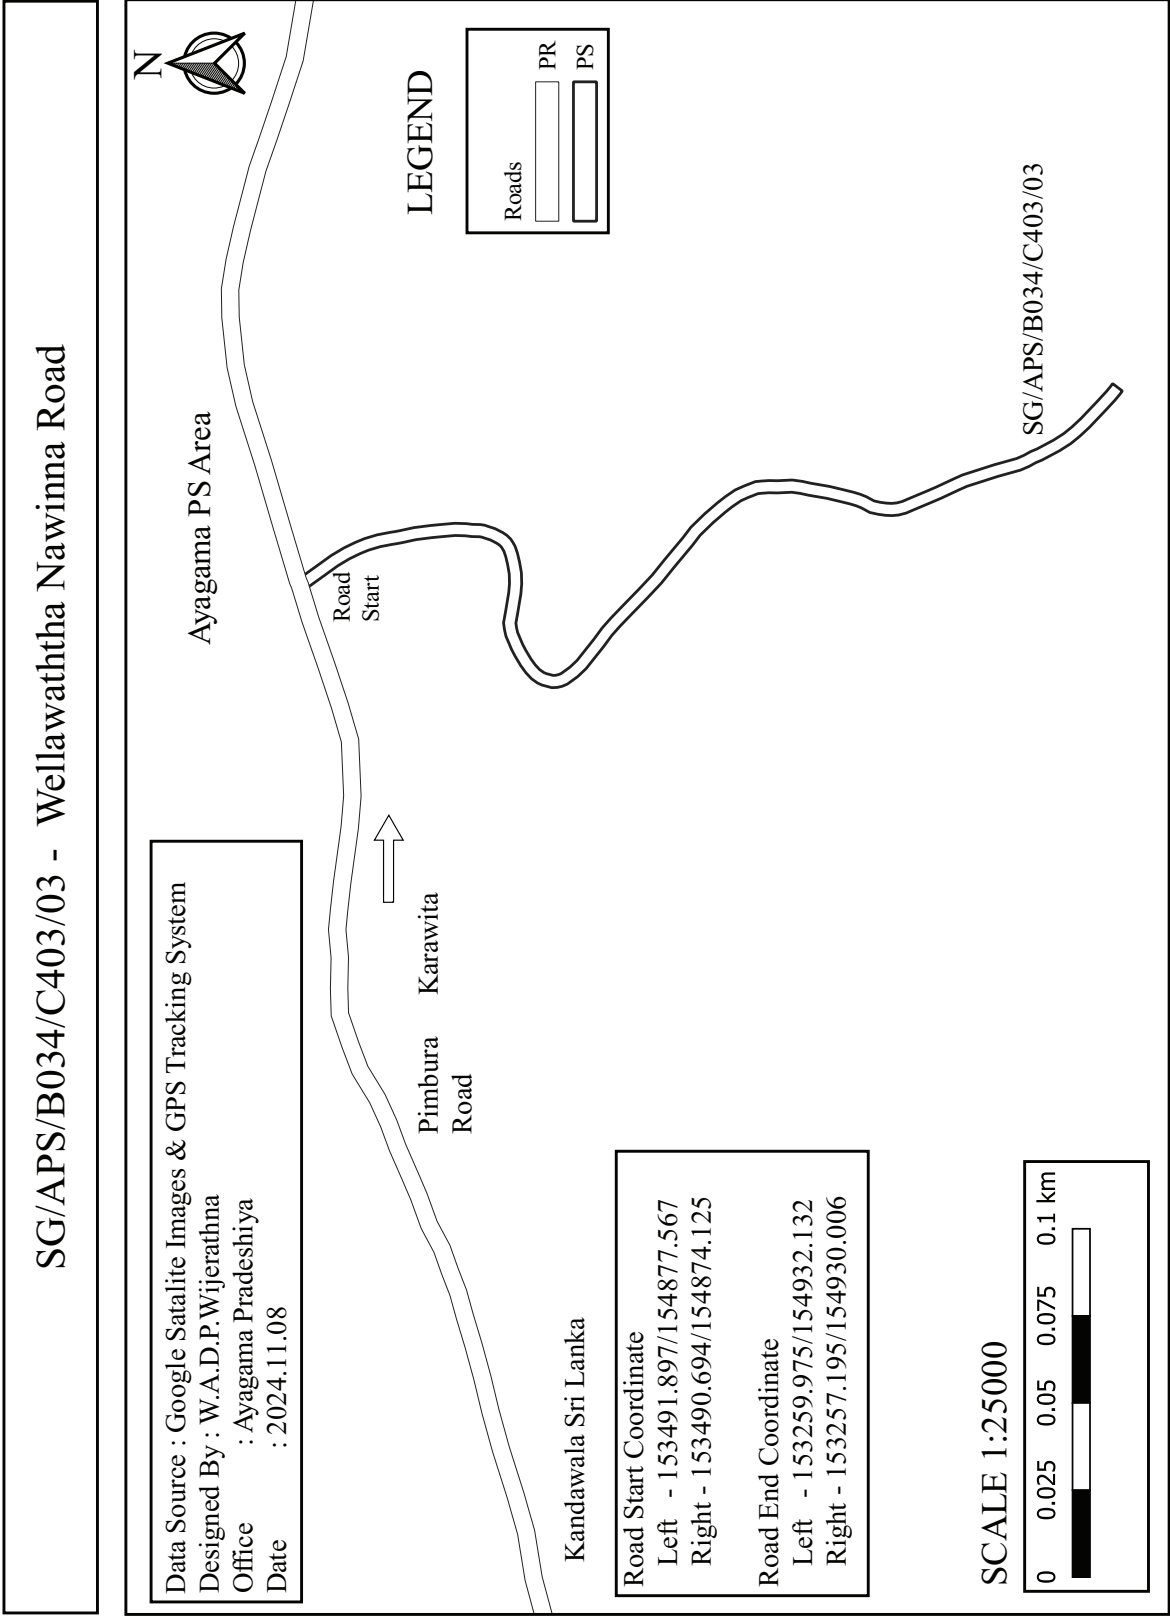


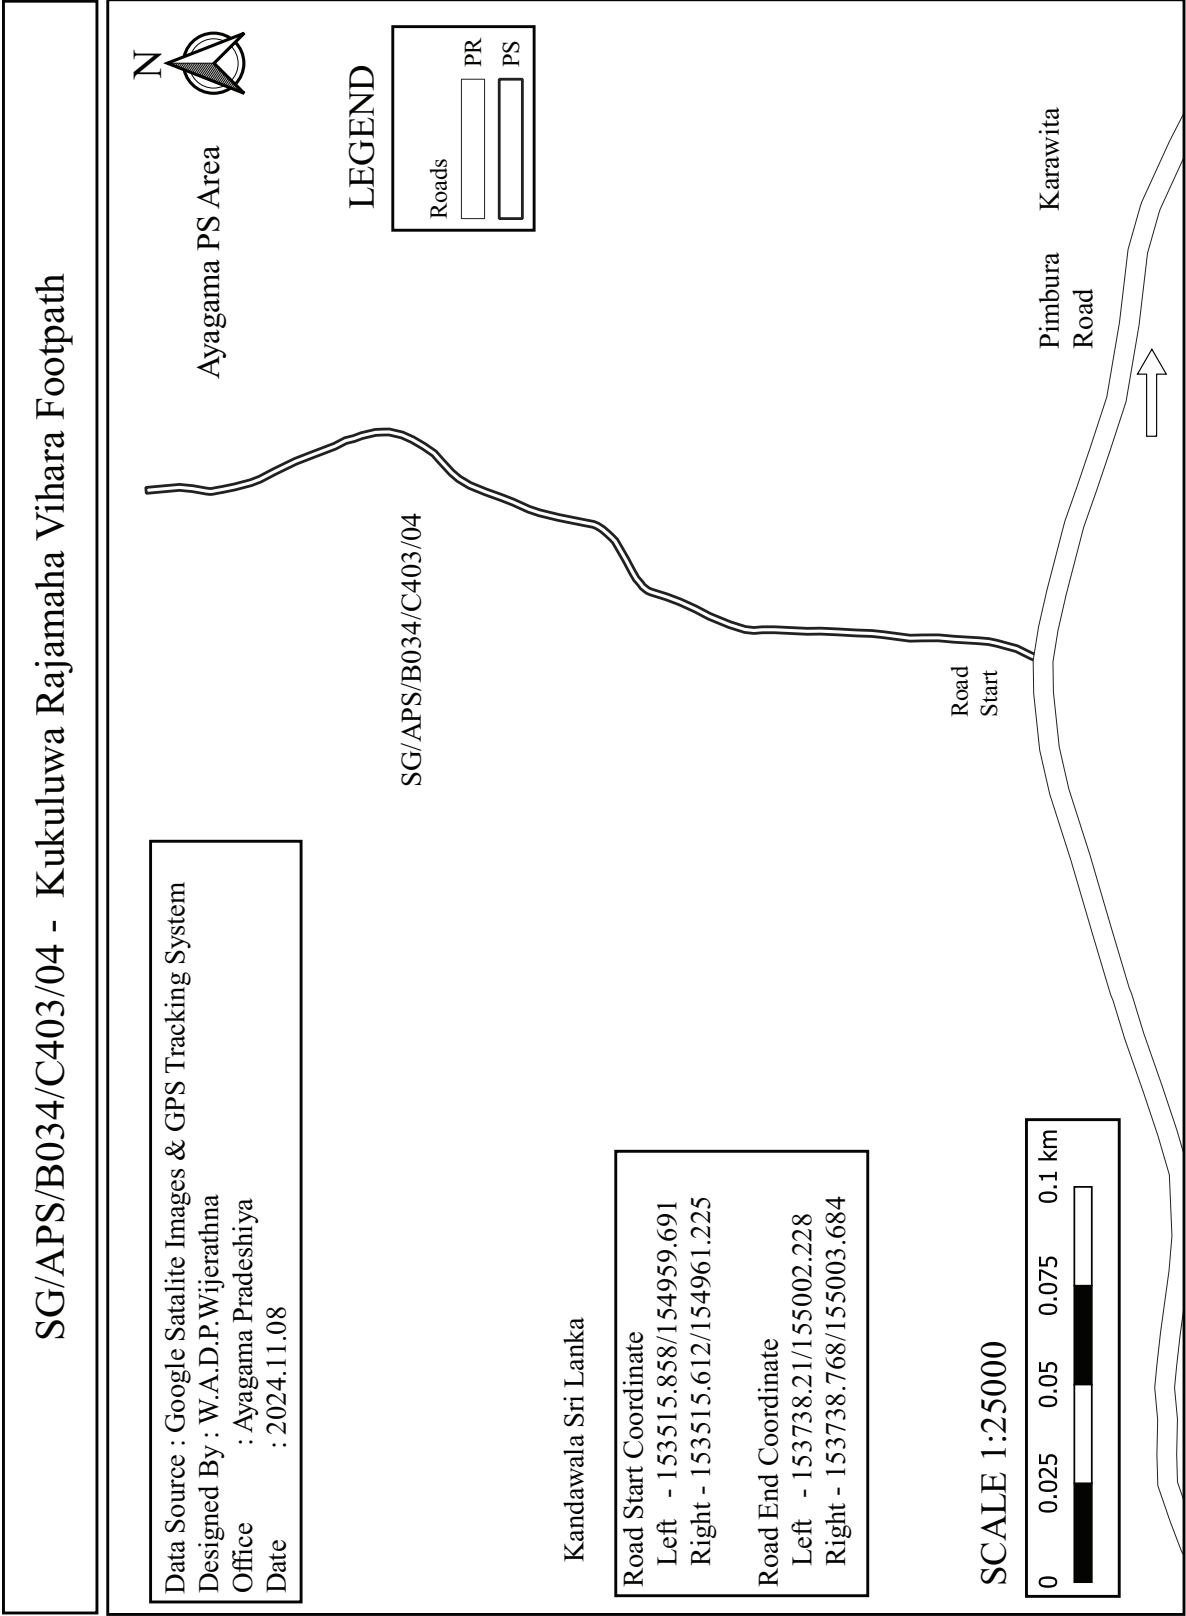


SG/APS/B034/C403/05 - Nawinnawaththa Dewala Road

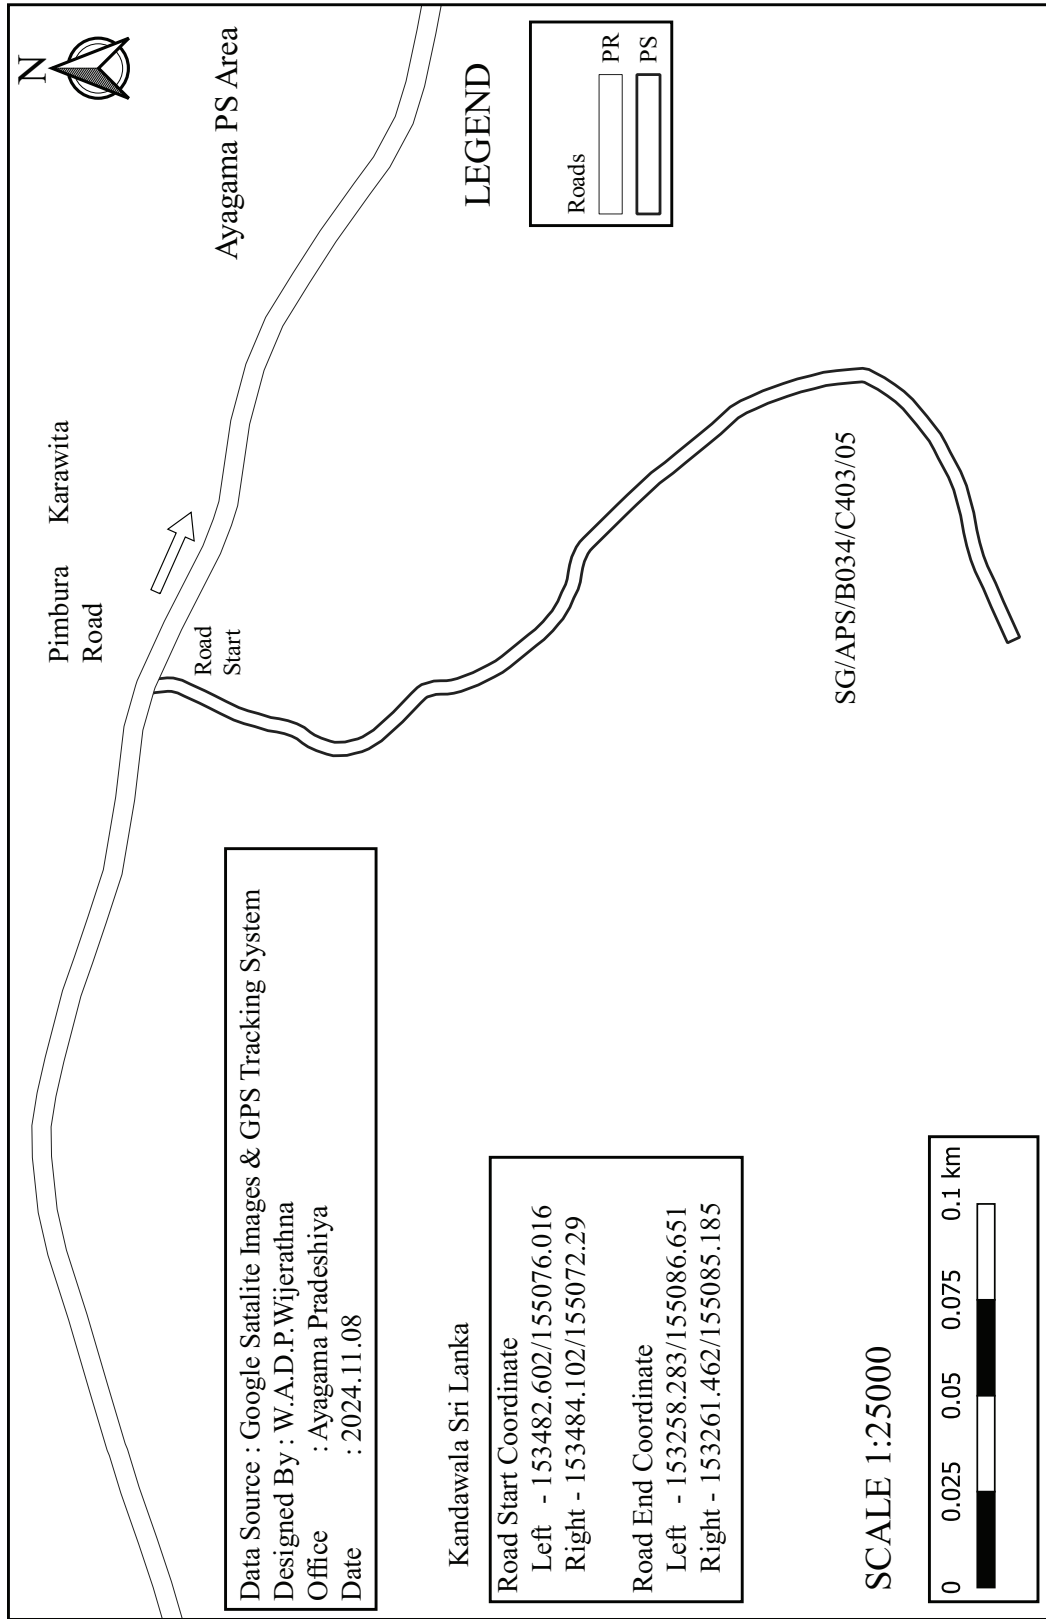


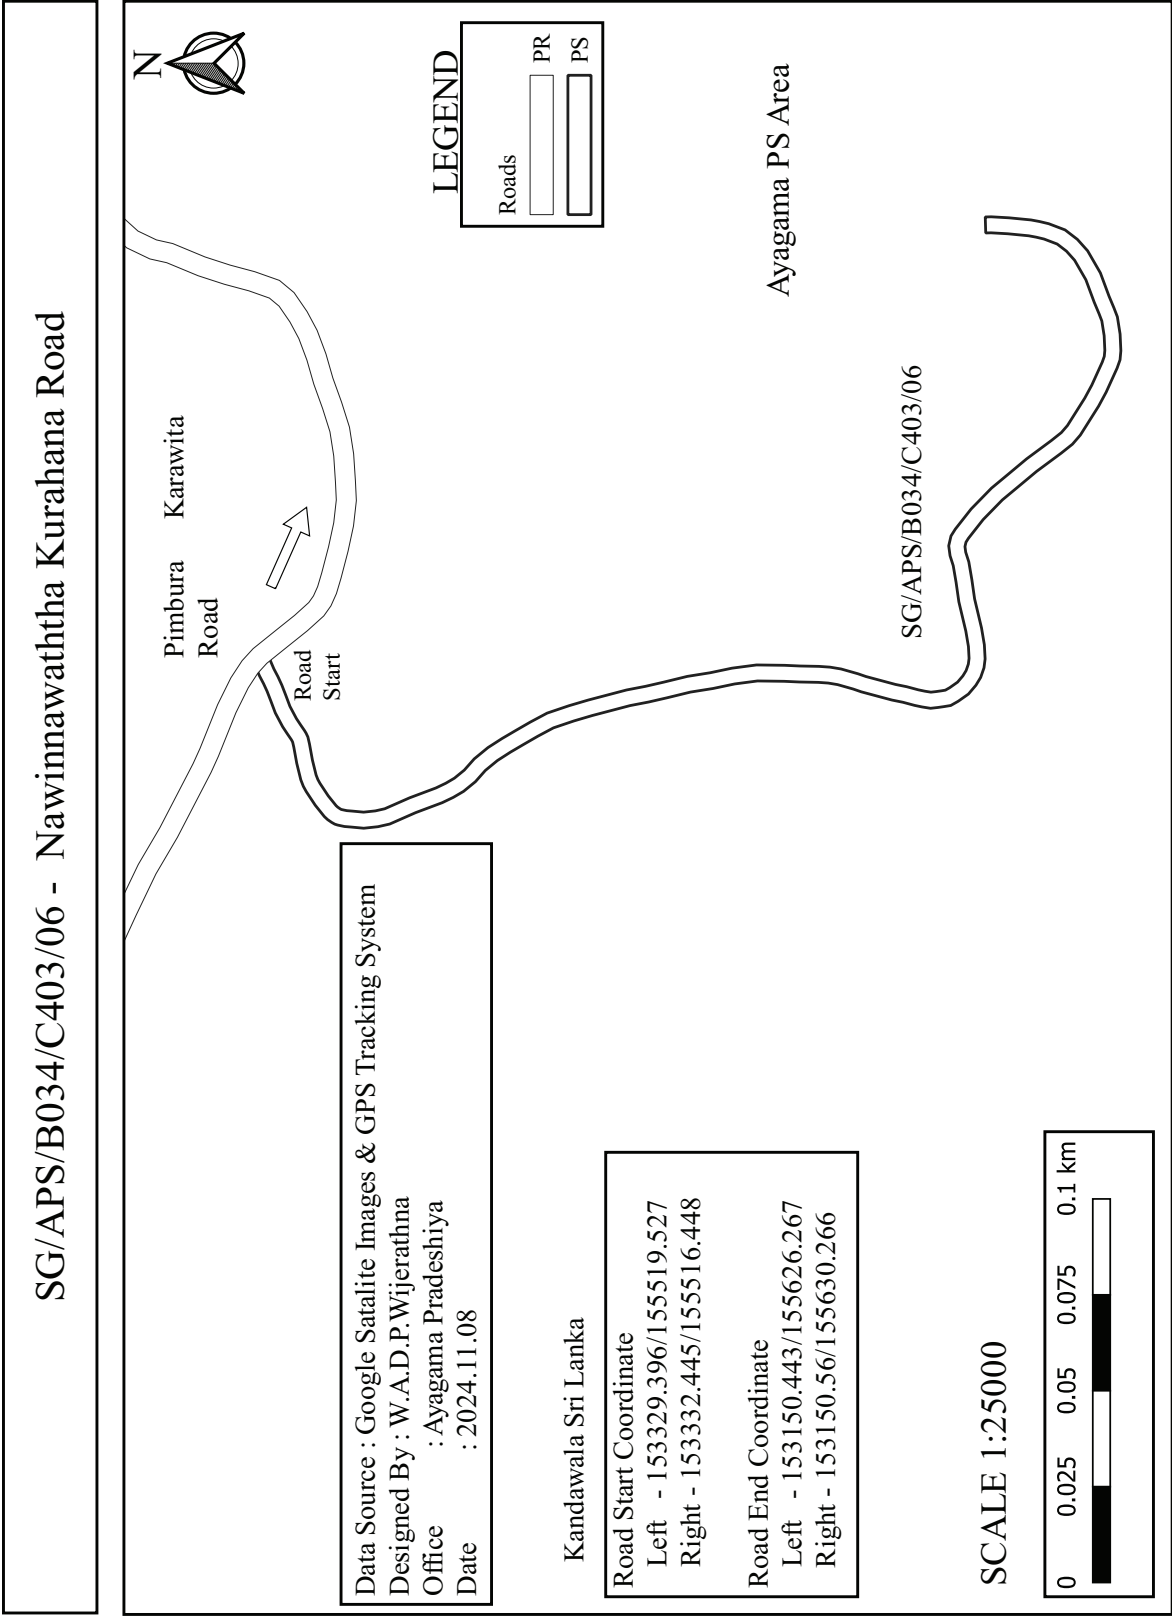


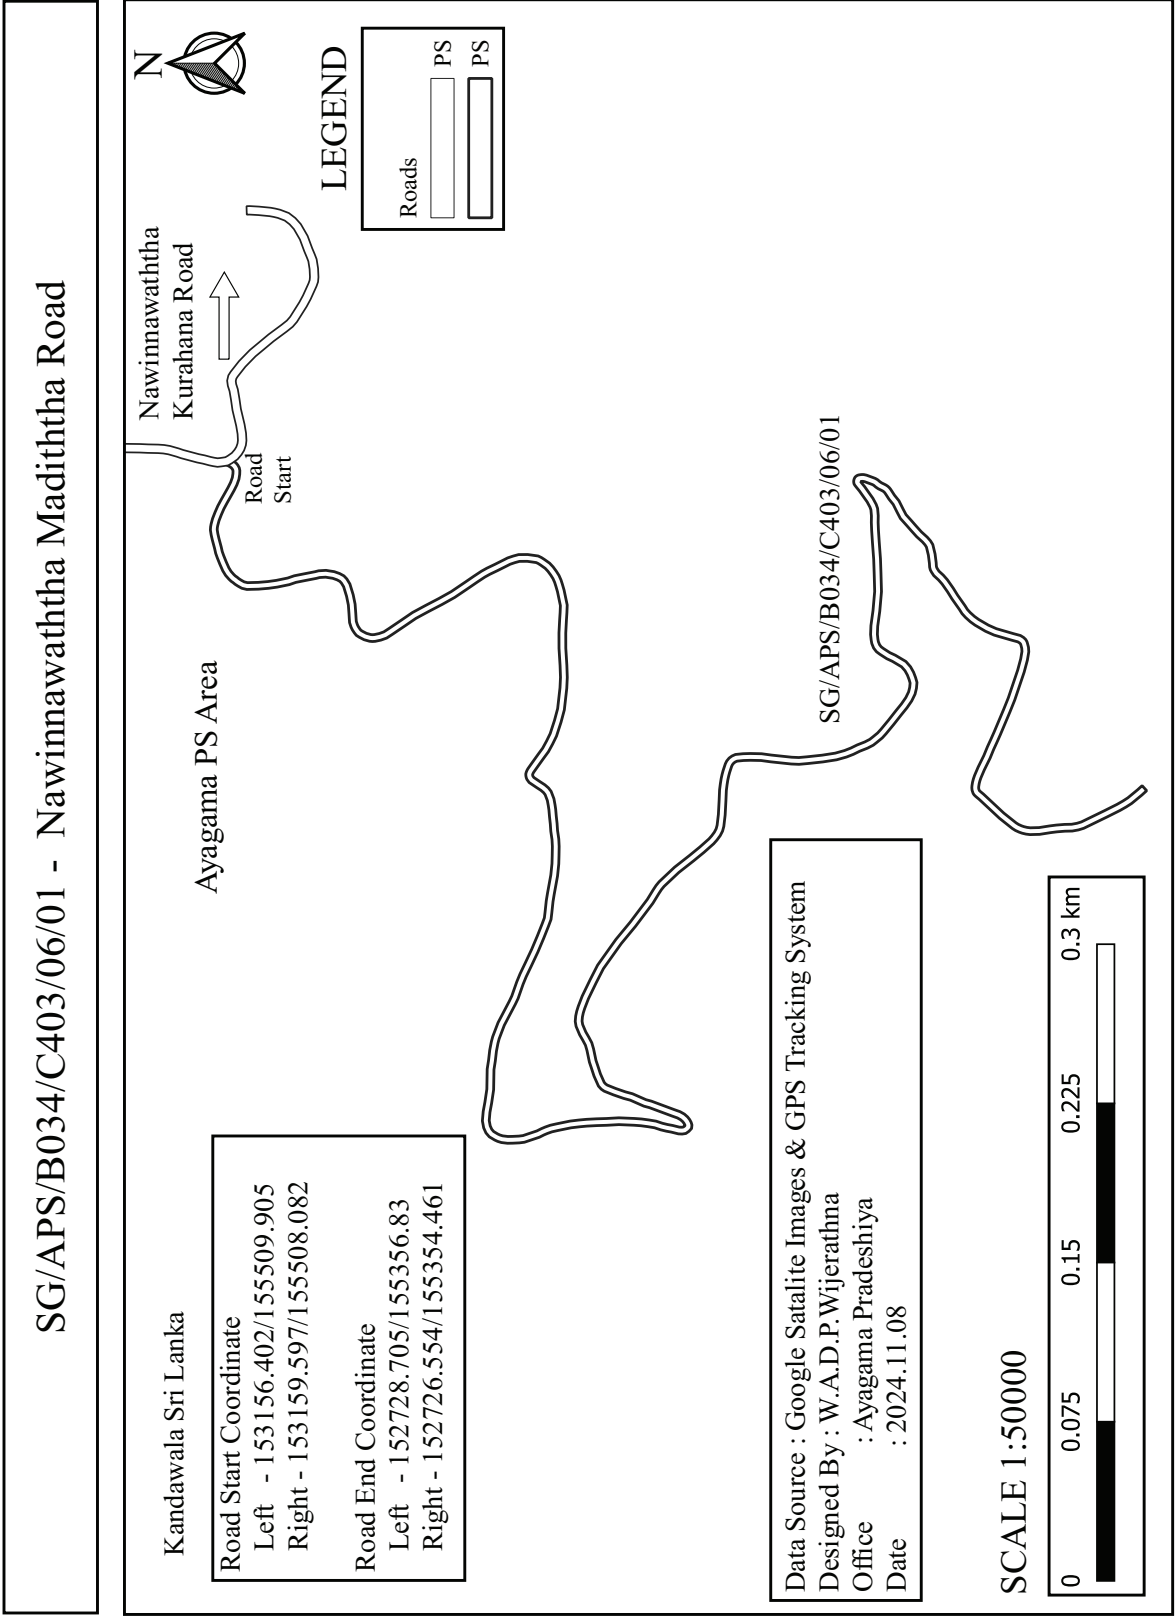


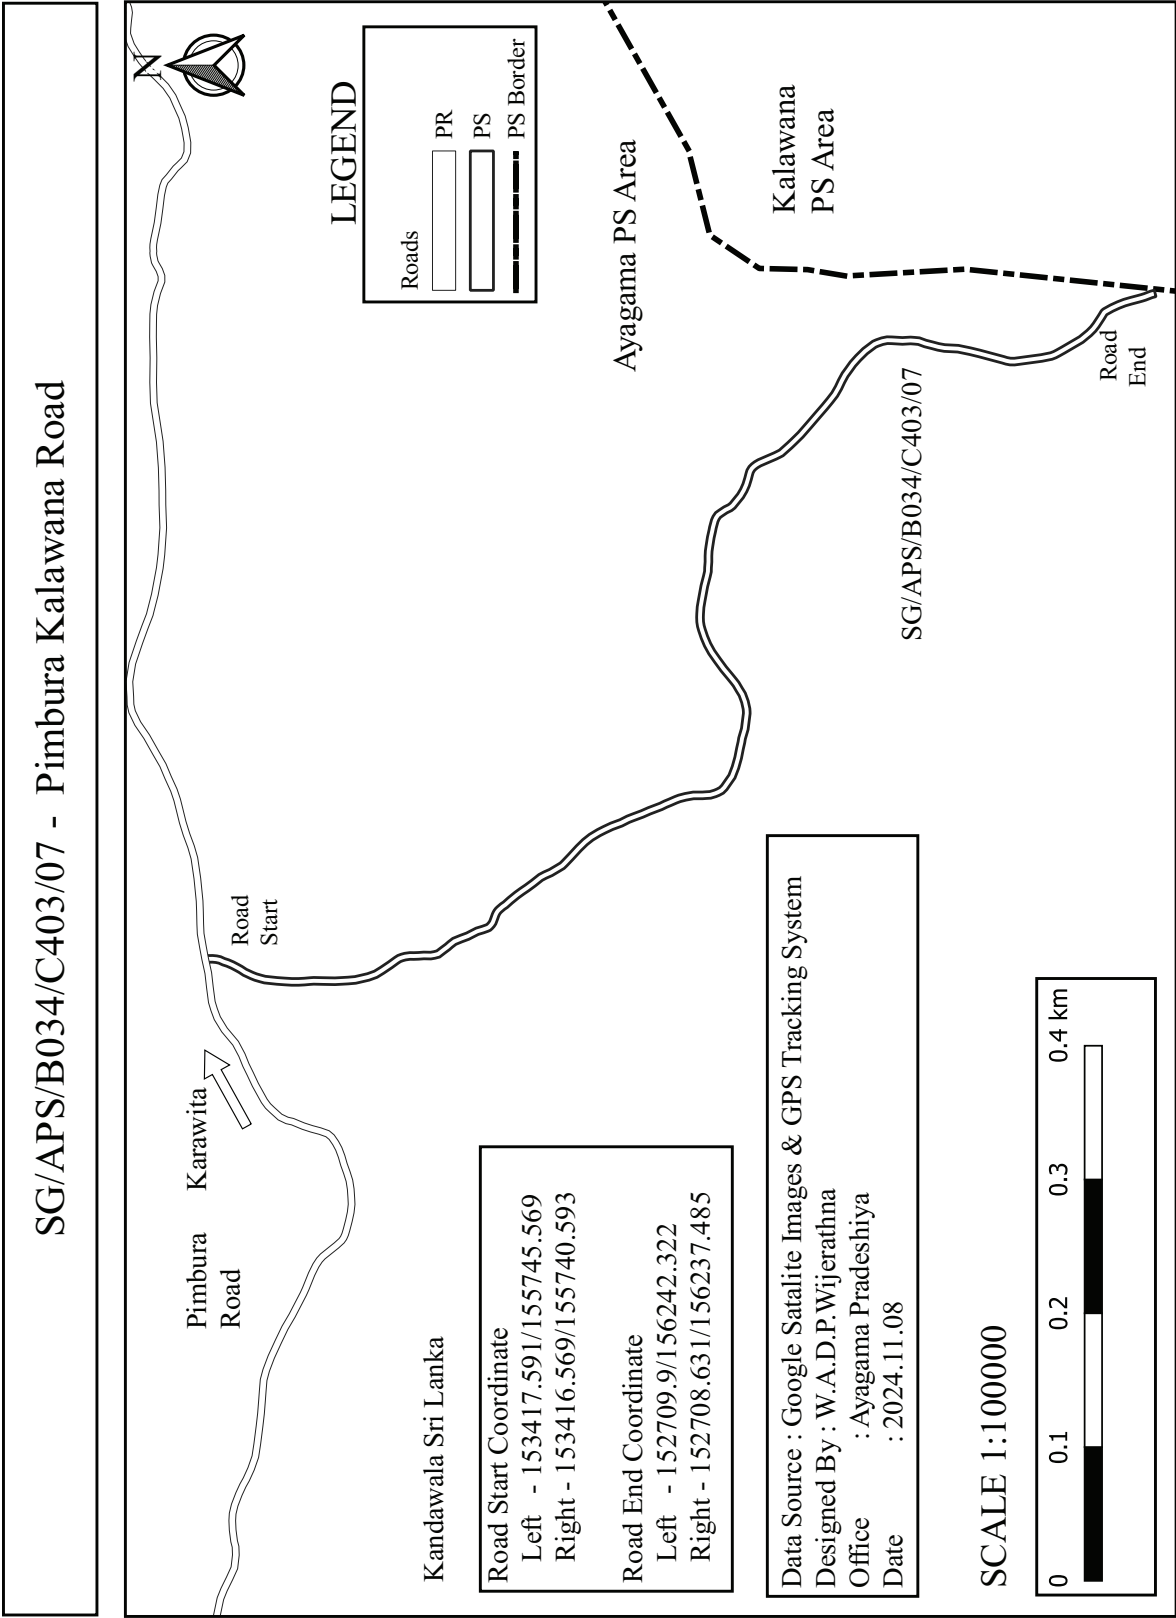


SG/APS/B034/C403/07/01 - Thennahena Road

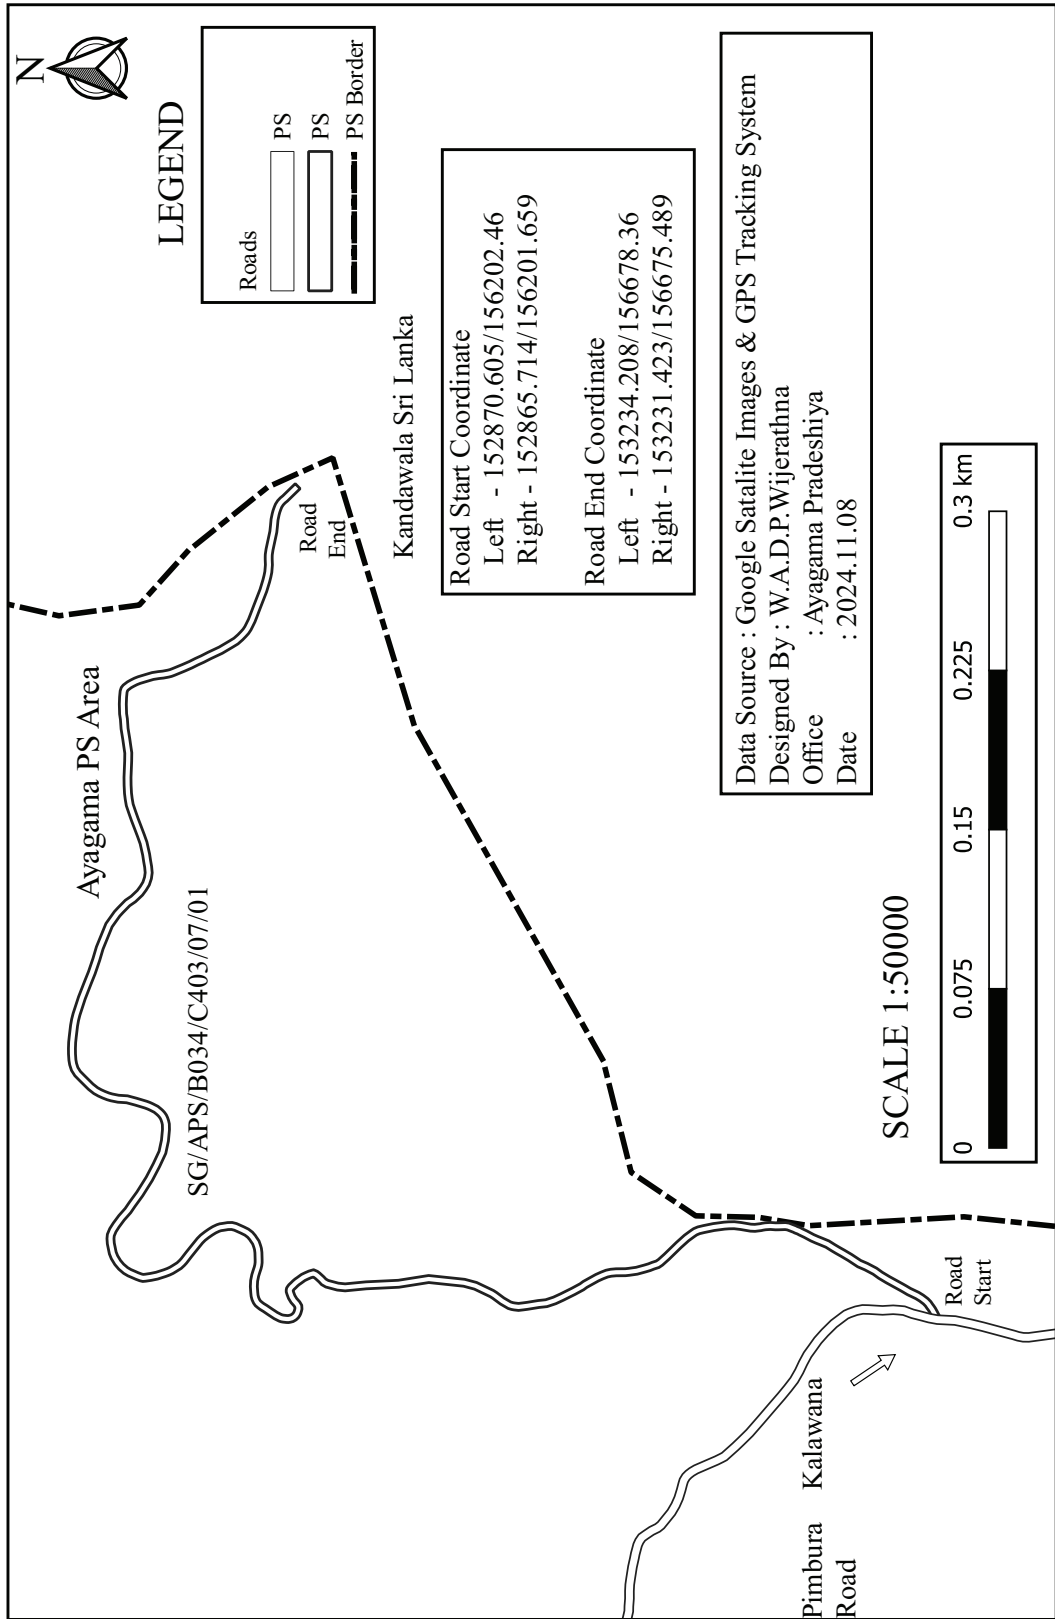

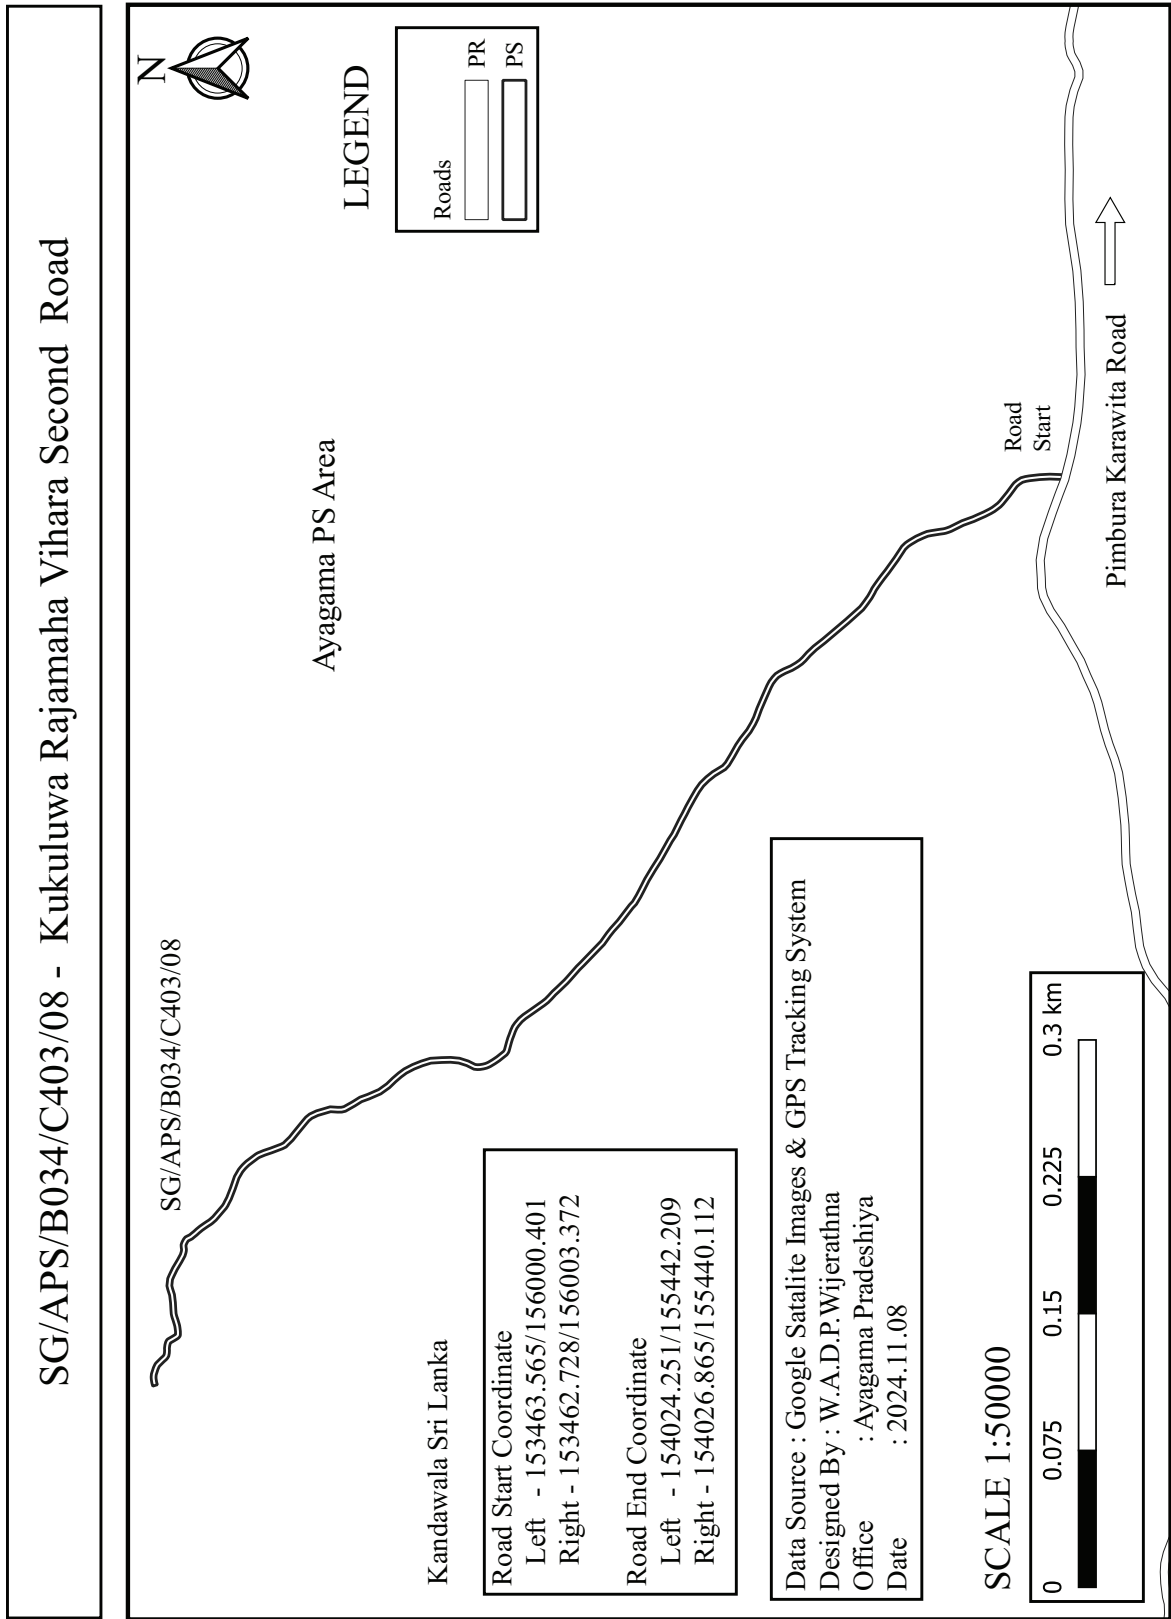

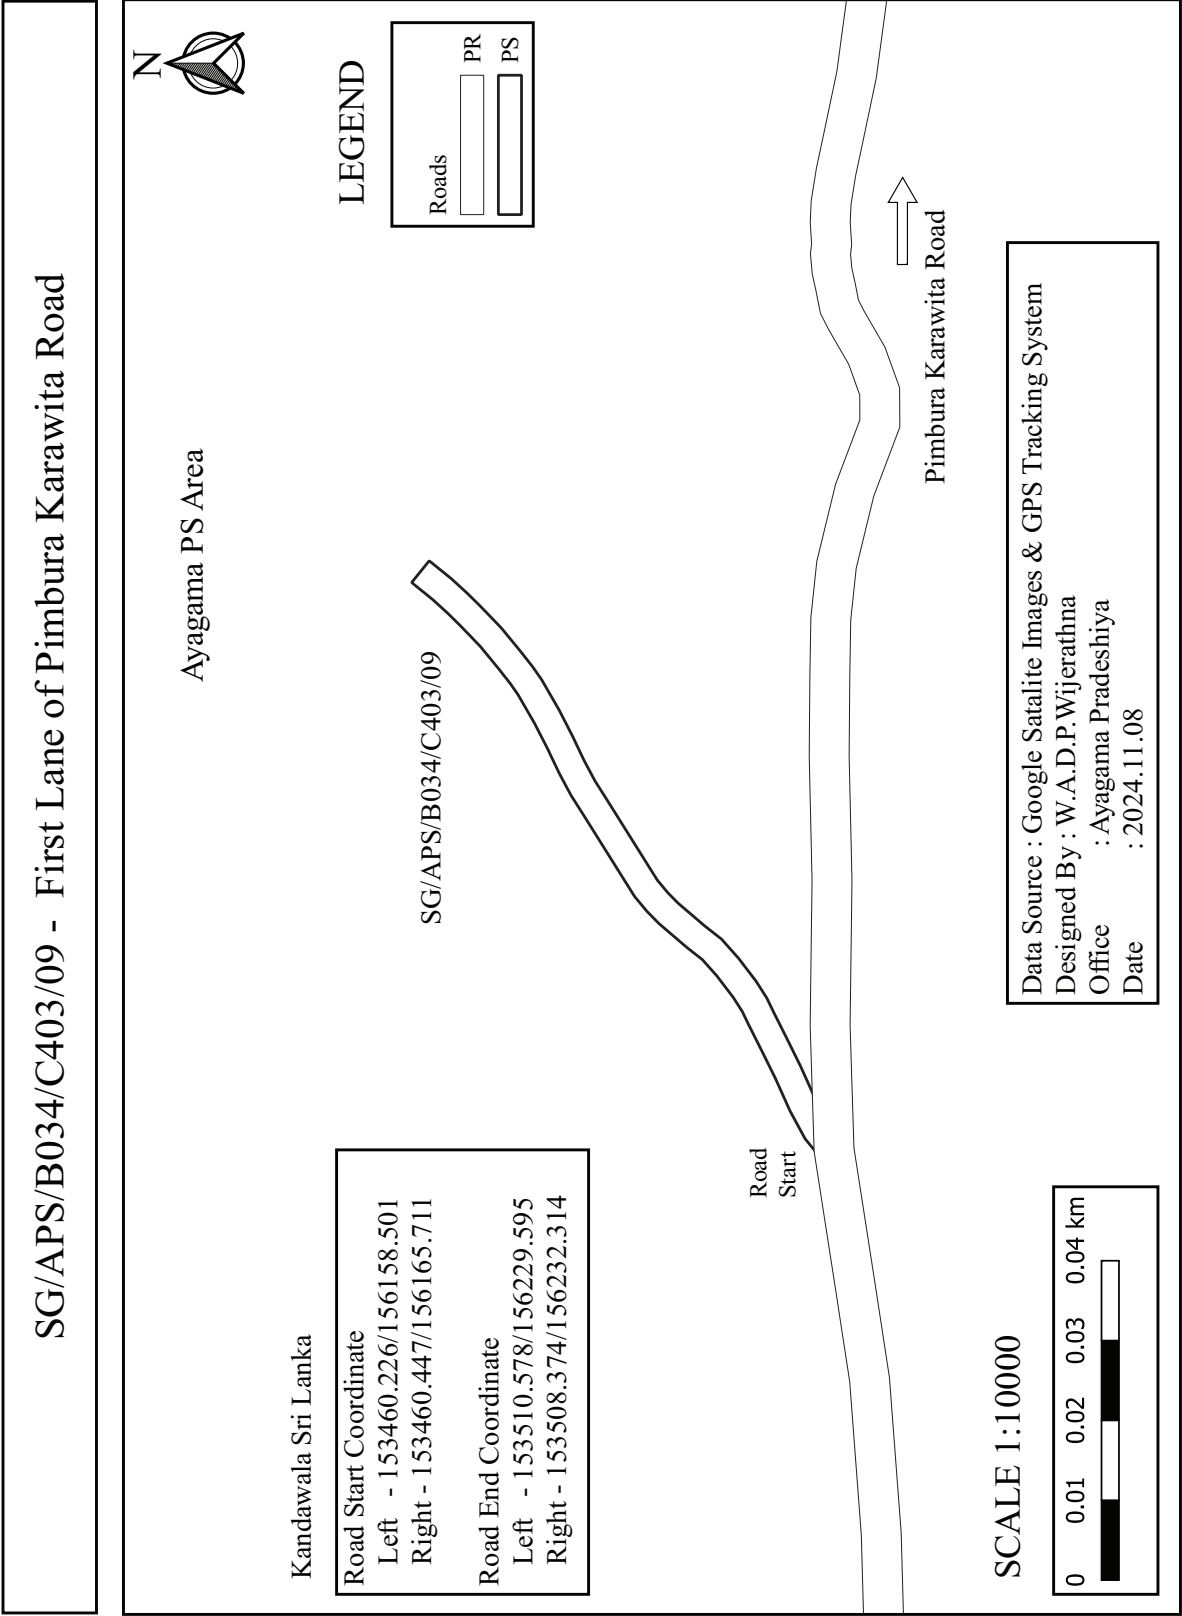

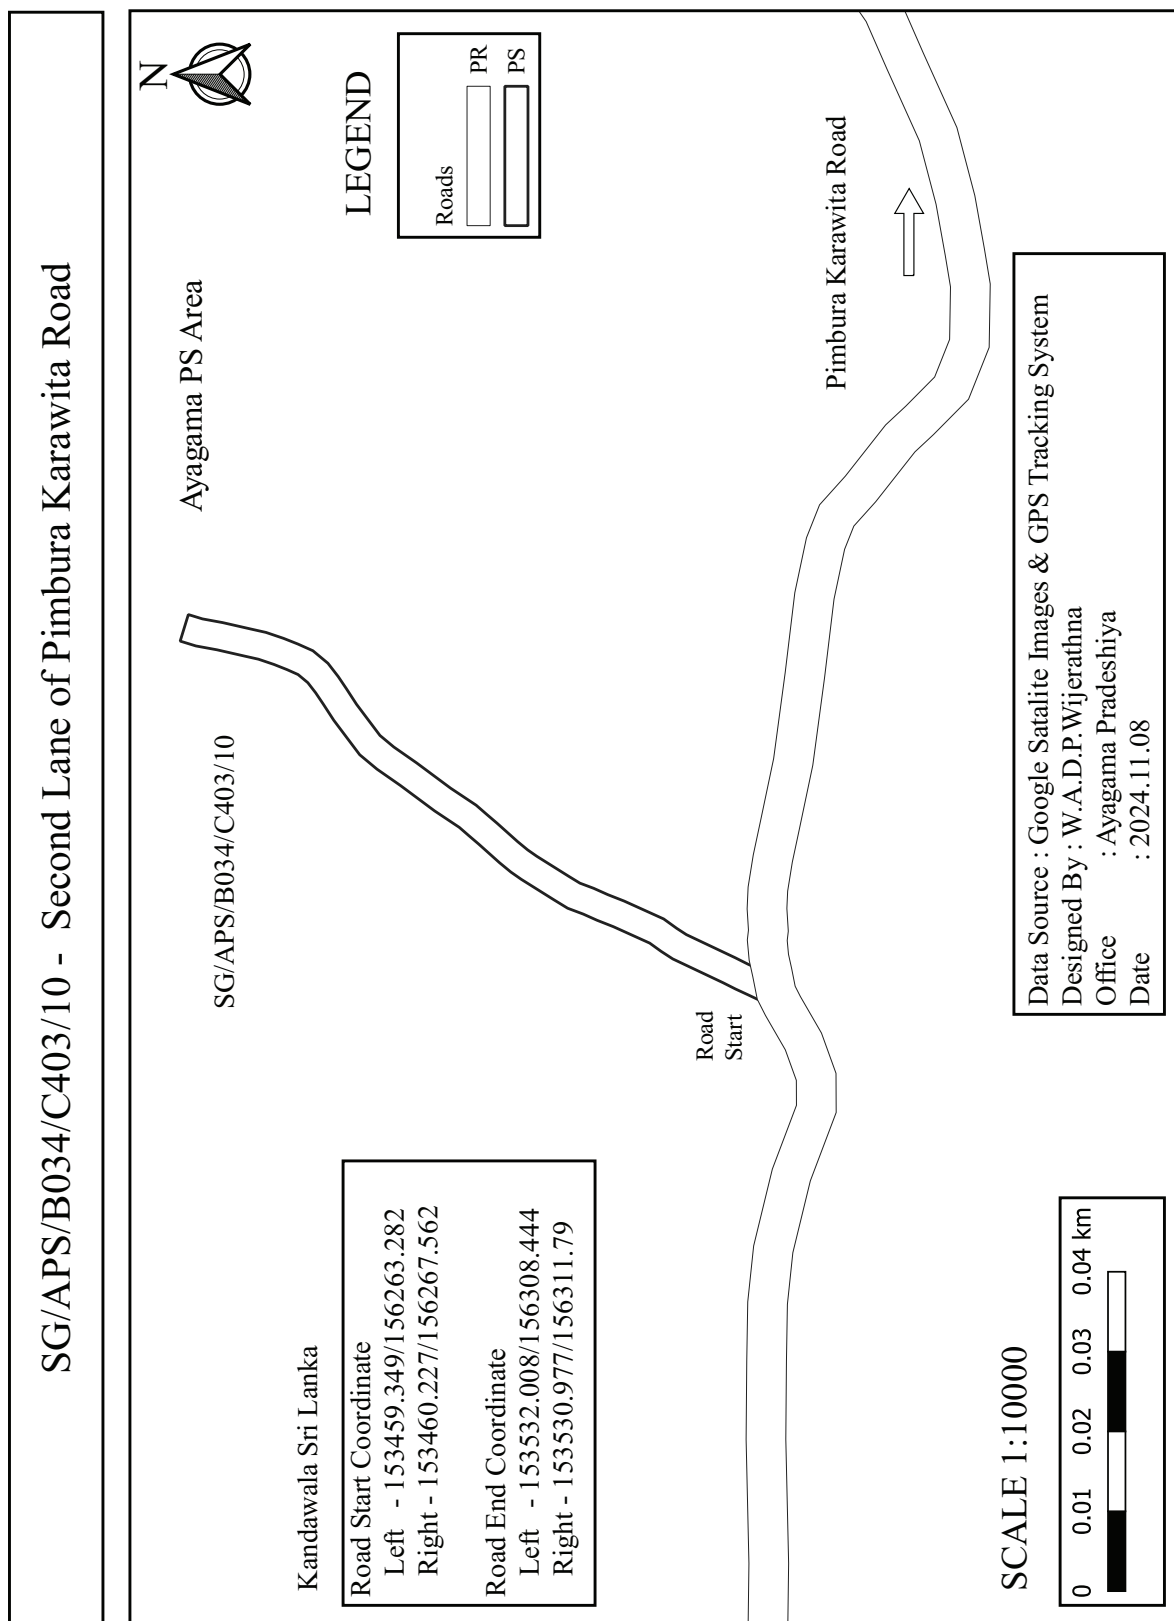

SG/APS/B421/C428/01 - First Lane of Kukulegama Jathuwangoda Road

