



ශ්‍රී ලංකා ප්‍රජාතාන්ත්‍රික සමාජවාදී ජනරජයේ ගැසට් පත්‍රය

අති විශේෂ

# The Gazette of the Democratic Socialist Republic of Sri Lanka

## EXTRAORDINARY

අංක 2414/05 - 2024 දෙසැම්බර් මස 10 වැනි අඟහරුවාදා - 2024.12.10  
No. 2414/05 - TUESDAY, DECEMBER 10, 2024

(Published by Authority)

## PART IV (B) — LOCAL GOVERNMENT

### Local Government Notification

#### AYAGAMA PRADESHIYA SABHA

AS per the function assigned to the Local Councils in Sabaragamuwa Province from “the order of the preparation of plans of roads and narrow lanes maintained by Pradeshiya Sabha in Sabaragamuwa Province and publication of notices showing the list of names” in Extraordinary *Gazette* No. 2316/20 and dated 24<sup>th</sup> January 2023 published by the Governor of Sabaragamuwa Province which should be read with Section 24 of Pradeshiya Sabha Act. No.15 of 1987, it is hereby notice to the public that the roads and narrow lanes included in the Schedule below should be declared as the roads and narrow lanes owned by the Ayagama Pradeshiya Sabha at its meeting under the decision No.03 and dated 20.06.2024.

And it is further notice that if it is the opinion of the party who is entitled to the said land, that any road or narrow lane included in the said Schedule go through, a case should be filed in the Court before the expiry of a period of three months from the date of this notice to prove the entitlement.

And it is further noticed that every road and narrow lane included in the said Schedule that cases are not assigned before the expiry of the said period of three months, are considered as a road or Narrow lane that owned by Ayagama Pradeshiya Sabha.

K. A. T. M. KUDA ARACHCHI,  
Secretary and Authorized Officer,  
Ayagama Pradeshiya Sabha.

Ayagama Pradeshiya Sabha,  
Ayagama,  
05th of December, 2024.



### List of Roads belonging to Ayagama Pradeshiya Sabha - Ayagama Kalawana Main Road

| Serial No. | Code of the Road     | Name of the Road                              | Starting Coordinates<br>(Kandawala Sri Lanka ) |                       | Ending Coordinates (Kandawala Sri Lanka ) |                       | Length of the Road (Meter) | Width of the Road (Meter) | Developed Width of the Road (Meter) |
|------------|----------------------|-----------------------------------------------|------------------------------------------------|-----------------------|-------------------------------------------|-----------------------|----------------------------|---------------------------|-------------------------------------|
|            |                      |                                               | Left                                           | Right                 | Left                                      | Right                 |                            |                           |                                     |
| 1          | SG/APS/B034/01       | Pelalimodarawaththa Road                      | 159876.947/148983.413                          | 159874.112/148984.555 | 159905.907/149885.744                     | 159906.975/149882.939 | 1352.2                     | 3.0                       |                                     |
| 2          | SG/APS/B034/01/01    | Pelalimodarawaththa Gamsabha Road             | 159877.497/149042.944                          | 159878.751/149049.381 | 160030.782/149513.286                     | 160027.886/149512.507 | 602.81                     | 3.0                       | 2.5                                 |
| 3          | SG/APS/B034/02       | Ayagama Akkara 08 Yakahatuwela Road           | 159776.853/149052.16                           | 159779.998/149049.682 | 160468.738/147891.991                     | 160465.818/147894.809 | 1857.53                    | 4.0                       | 3.0                                 |
| 4          | SG/APS/B034/02/01    | Mahaporuwakanda Road                          | 159735.011/149000.084                          | 159735.439/148996.823 | 159373.122/148527.286                     | 159375.522/148525.486 | 784.49                     | 3.0                       | 2.0                                 |
| 5          | SG/APS/B034/02/02    | Weraniyaketiya Road                           | 159881.887/148705.505                          | 159880.342/148701.478 | 159569.287/148483.953                     | 159571.939/148486.947 | 529.65                     | 4.0                       | 2.5                                 |
| 6          | SG/APS/B034/02/02/01 | First Lane of Weraniyaketiya Road             | 159700.651/148621.953                          | 159697.668/148622.287 | 159689.727/148674.064                     | 159686.763/148674.528 | 58.83                      | 3.0                       | 2.8                                 |
| 7          | SG/APS/B034/02/02/02 | Second Lane of Weraniyaketiya Road            | 159676.864/148629.875                          | 159670.766/148631.369 | 159648.827/148658.334                     | 159645.965/148659.235 | 46.61                      | 3.0                       | 3.0                                 |
| 8          | SG/APS/B034/02/03    | Akkara 08 Road                                | 159896.163/148288.035                          | 159893.565/148284.896 | 159044.8/148734.409                       | 159043.773/148730.109 | 993.24                     | 4.0                       | 3.5                                 |
| 9          | SG/APS/B034/02/04    | Waththainnakanda Pahala Road                  | 159879.35/148221.045                           | 159877.375/148218.784 | 159479.305/148252.167                     | 159476.739/148250.614 | 422.79                     | 3.0                       | 2.7                                 |
| 10         | SG/APS/B034/02/05    | Akkara 08 Waththainnakanda Road               | 159863.257/148197.441                          | 159863.872/148193.483 | 159857.93/147900.482                      | 159859.376/147904.212 | 435.75                     | 4.0                       | 3.0                                 |
| 11         | SG/APS/B034/02/05/01 | First Lane of Akkara 08 Waththainnakanda Road | 159717.39/148002.043                           | 159718.897/147999.446 | 159572.467/147803.659                     | 159574.459/147799.764 | 258.78                     | 3.0                       | 2.0                                 |
| 12         | SG/APS/B034/02/06    | Kithulgala Okanda Road                        | 159927.749/148107.283                          | 159930.172/148103.793 | 159847.958/148014.5                       | 159851.903/148015.158 | 129.72                     | 4.0                       | 3.0                                 |
| 13         | SG/APS/B034/02/07    | Waththainnakanda Pahala Road                  | 160406.523/147812.894                          | 160410.882/147813.516 | 159301.816/147931.145                     | 159305.283/147929.148 | 1514.7                     | 4.0                       | 3.5                                 |
| 14         | SG/APS/B034/02/07/01 | Kekunagahahena Road                           | 160409.473/147806.227                          | 160410.098/147810.406 | 160319.044/147126.992                     | 160322.993/147126.359 | 1036.92                    | 4.0                       | 3.5                                 |
| 15         | SG/APS/B034/02/07/02 | Sunimalaramaya Road                           | 160275.603/147707.697                          | 160279.735/147709.571 | 160452.02/147575.579                      | 160454.159/147578.349 | 228.15                     | 3.5                       | 2.6                                 |
| 16         | SG/APS/B034/02/07/03 | First Lane of Waththainnakanda Road           | 160123.442/147596.918                          | 160124.761/147599.693 | 160270.834/147498.315                     | 160271.575/147501.222 | 192.95                     | 3.0                       | 3.0                                 |

| Serial No. | Code of the Road     | Name of the Road                             | Starting Coordinates<br>(Kandawala Sri Lanka ) |                       | Ending Coordinates (Kandawala Sri Lanka ) |                       | Length of the Road (Meter) | Width of the Road (Meter) | Developed Width of the Road (Meter) |
|------------|----------------------|----------------------------------------------|------------------------------------------------|-----------------------|-------------------------------------------|-----------------------|----------------------------|---------------------------|-------------------------------------|
|            |                      |                                              | Left                                           | Right                 | Left                                      | Right                 |                            |                           |                                     |
| 17         | SG/APS/B034/02/07/04 | Malwela Sub Footpath                         | 160115.296/147583.669                          | 160117.421/147586.06  | 160080.563/147501.059                     | 160083.058/147499.39  | 116.49                     | 3.0                       | 2.0                                 |
| 18         | SG/APS/B034/02/07/05 | Waththainnakanda Kekunagahahena Road         | 160029.201/147534.248                          | 160032.641/147535.317 | 160417.467/147281.162                     | 160415.341/147284.577 | 520.85                     | 3.5                       | 3.0                                 |
| 19         | SG/APS/B034/03       | Veterinary Officer Office Road               | 159683.217/149143.266                          | 159678.225/149151.754 | 159574.286/149243.05                      | 159578.091/149243.562 | 217.39                     | 4.0                       | 3.0                                 |
| 20         | SG/APS/B034/04       | Nihathanigama Samarugama Thoranagoda Road    | 159499.955/149200.61                           | 159496.052/149199.269 | 159377.076/149566.606                     | 159379.326/149570.003 | 1401.66                    | 4.0                       | 3.5                                 |
| 21         | SG/APS/B034/04/01    | Sarathpuraya First Lane                      | 159471.165/149219.603                          | 159466.88/149220.591  | 159469.014/149295.972                     | 159465.021/149295.734 | 72.66                      | 4.0                       | 3.0                                 |
| 22         | SG/APS/B034/04/02    | Sarathpuraya Second Lane                     | 159392.077/149223.459                          | 159390.157/149224.139 | 159356.266/149288.908                     | 159352.841/149289.672 | 128.52                     | 2.0                       | 1.0                                 |
| 23         | SG/APS/B034/04/03    | Koratuwawaththa Road                         | 159250.253/149314.197                          | 159256.987/149315.207 | 159249.113/149289.054                     | 159251.528/149289.703 | 40.35                      | 2.5                       | 2.0                                 |
| 24         | SG/APS/B034/04/04    | The Road Leads from Sarathpuraya to Cemetery | 159117.957/149522.031                          | 159116.825/149524.857 | 159275.288/149566.638                     | 159273.2/149568.792   | 187.03                     | 3.0                       | 3.0                                 |
| 25         | SG/APS/B034/04/05    | Nihathanigama Pahala Wakra Road              | 159058.681/149552.921                          | 159061.605/149551.934 | 159020.189/149590.958                     | 159018.534/149593.463 | 460.36                     | 3.0                       | 3.0                                 |
| 26         | SG/APS/B034/04/06    | Nihathanigama Beraliyana Road                | 158983.715/149677.2                            | 158982.347/149673.256 | 158383.276/149913.921                     | 158381.918/149910.023 | 833.08                     | 4.0                       | 3.5                                 |
| 27         | SG/APS/B034/04/06/01 | Mahahena Waththa Road                        | 158964.351/149692.745                          | 158961.299/149694.296 | 158998.977/150099.954                     | 158996.351/150101.403 | 544.1                      | 3.0                       | 3.0                                 |
| 28         | SG/APS/B034/04/07    | Samarugama Cemetery Road                     | 159222.068/149663.818                          | 159222.56/149662.789  | 159167.768/149577.524                     | 159169.575/149577.603 | 109.07                     | 1.0                       | 1.0                                 |
| 29         | SG/APS/B034/05       | Akkara 17 Road                               | 159211.519/149034.985                          | 159218.216/149030.927 | 159041.303/148733.53                      | 159047.967/148731.88  | 414.34                     | 4.0                       | 3.0                                 |
| 30         | SG/APS/B034/05/01    | First Lane of Akkara 17 Road                 | 159130.998/148885.536                          | 159127.121/148884.22  | 159083.254/148926.653                     | 159080.254/148924.85  | 66.63                      | 3.5                       | 3.0                                 |
| 31         | SG/APS/B034/05/02    | Akkara 17 Uduwakkanda Road                   | 159044.8/148734.409                            | 159043.773/148730.109 | 158125.354/149478.274                     | 158121.421/149477.302 | 1973.6                     | 4.0                       | 3.0                                 |
| 32         | SG/APS/B034/05/02/01 | First Lane of Akkara 17 Uduwakkanda Road     | 159021.748/148734.947                          | 159025.062/148734.705 | 158796.759/148656.29                      | 158795.047/148653.825 | 470.44                     | 3.0                       | 2.0                                 |

| Serial No. | Code of the Road            | Name of the Road                                                 | Starting Coordinates<br>(Kandawala Sri Lanka ) |                       | Ending Coordinates<br>(Kandawala Sri Lanka ) |                       | Length of the Road<br>(Meter) | Width of the Road<br>(Meter) | Developed Width<br>of the Road (Meter) |
|------------|-----------------------------|------------------------------------------------------------------|------------------------------------------------|-----------------------|----------------------------------------------|-----------------------|-------------------------------|------------------------------|----------------------------------------|
|            |                             |                                                                  | Left                                           | Right                 | Left                                         | Right                 |                               |                              |                                        |
| 33         | SG/APS/<br>B034/05/02/01/01 | First By Pass of First<br>Lane of Akkara 17<br>Uduwakkanda Road  | 158991.422/148548.772                          | 158992.385/148549.052 | 159057.796/148519.906                        | 159058.97/148519.778  | 84.02                         | 1.0                          | 1.0                                    |
| 34         | SG/APS/<br>B034/05/02/02    | Akkara 17 Baligala<br>Thalapathgala Road                         | 158790.021/148650.333                          | 158794.837/148653.525 | 158382.198/147780.059                        | 158385.922/147778.599 | 1370.58                       | 4.0                          | 3.0                                    |
| 35         | SG/APS/<br>B034/05/02/02/01 | First Lane of<br>Akkara 17 Baligala<br>Thalapathgala Road        | 158817.423/148519.898                          | 158817.439/148528.493 | 158838.804/148127.09                         | 158822.184/148132.745 | 639.36                        | 4.0                          | 3.0                                    |
| 36         | SG/APS/<br>B034/05/02/03    | Second Lane of<br>Akkara 17<br>Uduwakkanda Road                  | 158438.414/148763.884                          | 158435.909/148765.709 | 158503.197/148862.357                        | 158500.647/148860.779 | 128.87                        | 3.0                          | 3.0                                    |
| 37         | SG/APS/B034/06              | Ereporuwa First Lane                                             | 158948.58/149198.35                            | 158950.482/149197.656 | 158925.977/149044.689                        | 158927.188/149046.282 | 175.85                        | 2.0                          | 2.0                                    |
| 38         | SG/APS/B034/07              | Hangamulla<br>Ereporuwa Road                                     | 158756.919/149280.358                          | 158751.859/149280.624 | 158853.235/149666.474                        | 158851.455/149670.328 | 493.5                         | 4.0                          | 3.0                                    |
| 39         | SG/APS/B034/08              | Bathalawaththa Road                                              | 158734.228/149276.134                          | 158737.683/149275.567 | 159079.02/148828.925                         | 159080.342/148832.184 | 641.26                        | 3.5                          | 3.0                                    |
| 40         | SG/APS/B034/09              | Beraliyana<br>Negirikanda Road                                   | 158343.692/149536.821                          | 158333.851/149536.613 | 157532.409/151660.94                         | 157528.419/151661.227 | 3194.99                       | 4.0                          | 3.0                                    |
| 41         | SG/APS/B034/09/01           | First Lane of<br>Beraliyana<br>Negirikanda Road                  | 158588.658/150216.398                          | 158590.104/150219.052 | 158692.325/150185.096                        | 158693.417/150187.89  | 110.23                        | 3.0                          | 2.0                                    |
| 42         | SG/APS/B034/09/02           | Second Lane of<br>Beraliyana<br>Negirikanda Road                 | 158627.329/150277.199                          | 158626.656/150280.344 | 158689.683/150433.452                        | 158692.408/150432.198 | 351.56                        | 3.0                          | 3.0                                    |
| 43         | SG/APS/B034/09/03           | Third Lane of<br>Beraliyana<br>Negirikanda Road                  | 158111.976/150987.353                          | 158112.465/150991.438 | 158275.157/151205.948                        | 158271.209/151206.585 | 306.03                        | 4.0                          | 3.0                                    |
| 44         | SG/APS/<br>B034/09/03/01    | First By Pass of First<br>Lane of Beraliyana<br>Negirikanda Road | 158154.744/150992.508                          | 158156.61/150997.015  | 158299.236/150956.415                        | 158301.233/150959.881 | 161.88                        | 4.0                          | 3.0                                    |
| 45         | SG/APS/B034/09/04           | Fourth Lane of<br>Beraliyana Negirikanda<br>Road                 | 157834.276/151232.737                          | 157836.717/151228.902 | 157712.493/151213.456                        | 157714.3/151209.888   | 141.11                        | 4.0                          | 4.0                                    |
| 46         | SG/APS/B034/09/05           | Fifth Lane of<br>Beraliyana<br>Negirikanda Road                  | 157738.073/151409.432                          | 157739.279/151405.489 | 157651.773/151359.443                        | 157651.821/151355.433 | 103.89                        | 4.0                          | 4.0                                    |



| Serial No. | Code of the Road     | Name of the Road                                   | Starting Coordinates<br>(Kandawala Sri Lanka ) |                       | Ending Coordinates (Kandawala Sri Lanka ) |                       | Length of the Road (Meter) | Width of the Road (Meter) | Developed Width of the Road (Meter) |
|------------|----------------------|----------------------------------------------------|------------------------------------------------|-----------------------|-------------------------------------------|-----------------------|----------------------------|---------------------------|-------------------------------------|
|            |                      |                                                    | Left                                           | Right                 | Left                                      | Right                 |                            |                           |                                     |
| 47         | SG/APS/B034/09/06    | Sixth Lane of Beraliyana Negirikanda Road          | 157740.857/151414.172                          | 157738.739/151412.038 | 157645.585/151601.7                       | 157643.157/151603.606 | 236.88                     | 3.0                       | 3.0                                 |
| 48         | SG/APS/B034/10       | Road from Madanagoda to Udugala                    | 158181.837/149530.177                          | 158184.494/149528.738 | 157391.423/149936.971                     | 157396.102/149933.757 | 1022.88                    | 3.0                       | 3.0                                 |
| 49         | SG/APS/B034/10/01    | First Lane of Road from Madanagoda to Udugala      | 158011.146/149532.548                          | 158013.627/149532.226 | 158005.128/149421.695                     | 158007.541/149422.344 | 137.14                     | 2.5                       | 2.5                                 |
| 50         | SG/APS/B034/10/02    | First Lane of Paragala Owita                       | 157873.215/149556.686                          | 157875.354/149554.572 | 157702.551/149441.812                     | 157700.574/149439.557 | 230.08                     | 3.0                       | 3.0                                 |
| 51         | SG/APS/B034/10/02/01 | By Pass of First Lane of Paragala Owita            | 157863.022/149546.611                          | 157866.47/149548.22   | 157875.338/149462.628                     | 157875.905/149465.575 | 94.72                      | 3.0                       | 3.0                                 |
| 52         | SG/APS/B034/10/03    | Second Lane of Paragala Owita                      | 157834.076/149624.615                          | 157835.474/149621.555 | 157643.499/149637.885                     | 157644.625/149635.105 | 203.97                     | 3.0                       | 3.0                                 |
| 53         | SG/APS/B034/10/04    | Second Lane of the Road from Madanagoda to Udugala | 157572.746/149848.72                           | 157574.867/149848.169 | 157407.661/149823.444                     | 157411.3/149823.103   | 209.54                     | 2.0                       | 2.0                                 |
| 54         | SG/APS/B034/11       | Siriwardhanawaththa First Road                     | 158119.974/149611.359                          | 158117.772/149613.678 | 158097.966/150266.167                     | 158097.965/150269.167 | 797                        | 3.0                       | 3.0                                 |
| 55         | SG/APS/B034/11/01    | First Lane of Siriwardhanawaththa First Road       | 158165.277/149982.886                          | 158164.765/149979.875 | 158001.442/150157.23                      | 158000.977/150154.266 | 278.05                     | 3.0                       | 3.0                                 |
| 56         | SG/APS/B034/11/02    | Second Lane of Siriwardhanawaththa First Road      | 158183.877/150138.891                          | 158183.701/150135.855 | 158056.203/150194.002                     | 158054.299/150191.685 | 155.02                     | 3.0                       | 2.0                                 |
| 57         | SG/APS/B034/12       | Siriwardhanawaththa Second Road                    | 158067.32/149668.969                           | 158064.904/149672.168 | 158155.149/149764.095                     | 158152.044/149766.619 | 132.98                     | 4.0                       | 3.7                                 |
| 58         | SG/APS/B034/13       | Siriwardhanawaththa Third Road                     | 157819.709/149904.392                          | 157818.331/149909.932 | 157908.052/149997.177                     | 157909.043/150000.008 | 188.4                      | 3.0                       | 3.0                                 |
| 59         | SG/APS/B034/14       | Kekulama Road                                      | 157692.678/150117.011                          | 157690.766/150120.01  | 157859.924/150207.02                      | 157859.935/150210.02  | 209.84                     | 3.0                       | 2.5                                 |
| 60         | SG/APS/B034/15       | Udugala 700 Waththa Road                           | 157472.011/150400.013                          | 157465.682/150409.027 | 158082.002/150937.345                     | 158082.049/150940.482 | 1152.86                    | 3.0                       | 2.6                                 |
| 61         | SG/APS/B034/16       | Udugala Cemetery Road                              | 157213.578/150638.917                          | 157209.917/150640.688 | 157473.954/150759.872                     | 157471.31/150762.871  | 441.99                     | 4.0                       | 3.0                                 |
| 62         | SG/APS/B034/16/01    | First Lane of Udugala Cemetery Road                | 157441.317/150680.703                          | 157443.508/150682.996 | 157490.669/150671.598                     | 157491.717/150674.145 | 55.95                      | 2.8                       | 2.8                                 |

| Serial No. | Code of the Road     | Name of the Road                            | Starting Coordinates<br>(Kandawala Sri Lanka ) |                       | Ending Coordinates<br>(Kandawala Sri Lanka ) |                       | Length of the Road<br>(Meter) | Width of the Road<br>(Meter) | Developed Width<br>of the Road (Meter) |
|------------|----------------------|---------------------------------------------|------------------------------------------------|-----------------------|----------------------------------------------|-----------------------|-------------------------------|------------------------------|----------------------------------------|
|            |                      |                                             | Left                                           | Right                 | Left                                         | Right                 |                               |                              |                                        |
| 63         | SG/APS/B034/17       | Udugala New Colony Road                     | 157184.913/150645.936                          | 157180.588/150644.712 | 157214.234/151039.016                        | 157211.488/151036.106 | 537.82                        | 4.0                          | 3.0                                    |
| 64         | SG/APS/B034/17/01    | First Lane of Udugala New Colony Road       | 157136.225/150717.328                          | 157134.024/150715.029 | 157115.616/150802.37                         | 157112.682/150802.997 | 126.93                        | 3.0                          | 3.0                                    |
| 65         | SG/APS/B034/17/02    | Second Lane of Udugala New Colony Road      | 157194.701/150840.201                          | 157193.513/150842.97  | 157258.397/150834.561                        | 157258.816/150837.531 | 67.31                         | 3.0                          | 3.0                                    |
| 66         | SG/APS/B034/17/03    | Third Lane of Udugala New Colony Road       | 157179.764/150851.724                          | 157183.032/150849.121 | 157144.654/150802.344                        | 157146.314/150798.704 | 64.78                         | 4.0                          | 3.0                                    |
| 67         | SG/APS/B034/17/04    | Fourth Lane of Udugala New Colony Road      | 157200.963/150891.536                          | 157203.824/150894.019 | 157287.029/150857.015                        | 157287.488/150859.98  | 97.11                         | 3.0                          | 3.0                                    |
| 68         | SG/APS/B034/17/05    | Fifth Lane of Udugala New Colony Road       | 157216.086/150916.647                          | 157213.762/150913.39  | 157127.214/150981.919                        | 157125.388/150978.36  | 123.59                        | 4.0                          | 3.0                                    |
| 69         | SG/APS/B034/18       | Akkara 20 Road                              | 156877.268/150804.353                          | 156877.963/150800.9   | 156656.696/150684.219                        | 156654.526/150679.967 | 304.82                        | 3.5                          | 3.0                                    |
| 70         | SG/APS/B034/19       | Paragala Tea Factory Road                   | 156572.965/151531.534                          | 156566.092/151530.921 | 156786.029/151735.844                        | 156782.224/151737.077 | 510.48                        | 4.0                          | 3.5                                    |
| 71         | SG/APS/B034/20       | Manakanda Dawalaketiya Paragalawaththa Road | 156360.177/151676.944                          | 156359.953/151672.728 | 155883.786/151411.51                         | 155887.773/151411.84  | 611.81                        | 4.0                          | 2.6                                    |
| 72         | SG/APS/B034/20/01    | Paragala Kodigedarawaththa Road             | 156168.376/151640.022                          | 156171.544/151642.503 | 156236.059/151404.622                        | 156238.258/151401.282 | 358.16                        | 4.0                          | 2.5                                    |
| 73         | SG/APS/B034/20/02    | Paragala Manakanda Road                     | 156169.797/151646.132                          | 156166.453/151643.627 | 155789.695/151426.375                        | 155792.419/151429.304 | 593.3                         | 4.0                          | 2.5                                    |
| 74         | SG/APS/B034/20/02/01 | Paragala Keselkotuwa Road                   | 156157.289/151679.199                          | 156154.634/151682.46  | 156034.065/151783.759                        | 156034.102/151780.759 | 207.91                        | 3.0                          | 2.0                                    |
| 75         | SG/APS/B034/20/02/02 | First Lane of Paragala Manakanda Road       | 156010.801/151671.013                          | 156007.863/151670.303 | 155883.58/151868.857                         | 155881.899/151871.343 | 342.96                        | 3.0                          | 2.4                                    |
| 76         | SG/APS/B034/20/02/03 | Paragalakanda Road                          | 155843.954/151581.64                           | 155840.732/151579.269 | 155314.994/151842.066                        | 155311.916/151839.512 | 638.21                        | 4.0                          | 2.5                                    |
| 77         | SG/APS/B034/20/02/04 | Manakanda Paragalakanda Road                | 155772.657/151521.694                          | 155771.718/151517.214 | 155589.382/151354.958                        | 155591.602/151352.94  | 284.75                        | 3.0                          | 1.0                                    |
| 78         | SG/APS/B034/21       | Paragala Galaudakanda Niriella Road         | 156373.909/151711.103                          | 156373.201/151716.646 | 156792.033/153926.13                         | 156788.576/153926.675 | 2579.91                       | 3.5                          | 3.0                                    |

| Serial No. | Code of the Road         | Name of the Road                                     | Starting Coordinates<br>(Kandawala Sri Lanka ) |                       | Ending Coordinates (Kandawala Sri Lanka ) |                       | Length of the Road (Meter) | Width of the Road (Meter) | Developed Width of the Road (Meter) |
|------------|--------------------------|------------------------------------------------------|------------------------------------------------|-----------------------|-------------------------------------------|-----------------------|----------------------------|---------------------------|-------------------------------------|
|            |                          |                                                      | Left                                           | Right                 | Left                                      | Right                 |                            |                           |                                     |
| 79         | SG/APS/B034/21/01        | Kodikarapanguwa Road                                 | 156538.424/151964.35                           | 156536.76/151960.071  | 156381.863/151983.084                     | 156385.862/151982.999 | 214.84                     | 4.0                       | 2.5                                 |
| 80         | SG/APS/B034/21/02        | Kiwulahena<br>Kodikarapanguwa Road                   | 156546.391/152043.263                          | 156548.149/152048.114 | 156787.385/151893.95                      | 156791.09/151895.46   | 310.94                     | 4.0                       | 3.0                                 |
| 81         | SG/APS/<br>B034/21/02/01 | First Lane of<br>Kiwulahena<br>Kodikarapanguwa Road  | 156598.289/152032.348                          | 156594.757/152034.194 | 156898.787/152008.165                     | 156898.007/152011.062 | 321.58                     | 3.0                       | 2.0                                 |
| 82         | SG/APS/B034/21/03        | Galawudakanda First<br>Lane                          | 156571.617/152309.337                          | 156570.741/152312.83  | 156623.027/152278.37                      | 156626.563/152277.695 | 83.32                      | 3.6                       | 3.0                                 |
| 83         | SG/APS/B034/21/04        | Galawudakanda<br>Bathalawaththa Road                 | 156573.555/152773.207                          | 156574.564/152768.959 | 156404.175/152802.831                     | 156402.073/152799.428 | 188.43                     | 4.0                       | 3.5                                 |
| 84         | SG/APS/B034/21/05        | Paragala Galaudakanda<br>Niriella Aramba<br>Footpath | 156607.192/152840.292                          | 156608.18/152843.295  | 156645.905/152795.527                     | 156648.802/152796.306 | 65.93                      | 3.0                       | 2.5                                 |
| 85         | SG/APS/B034/22           | Paragala Amuhenkanda<br>Road                         | 156311.263/151852.193                          | 156308.847/151853.986 | 156339.724/151947.712                     | 156337.826/151949.633 | 114.43                     | 2.7                       | 2.5                                 |
| 86         | SG/APS/B034/23           | Paragala Amuhena<br>Road                             | 156018.482/152154.787                          | 156015.62/152153.686  | 156165.389/152193.153                     | 156167.56/152195.224  | 280.02                     | 3.0                       | 2.5                                 |
| 87         | SG/APS/B034/24           | Paragala Pokunudola<br>Road                          | 155906.959/152234.496                          | 155903.953/152235.52  | 156005.52/152398.007                      | 156004.741/152400.905 | 221.13                     | 3.0                       | 2.5                                 |
| 88         | SG/APS/B034/25           | Paragala Kirimethena<br>Road                         | 155605.488/152254.823                          | 155610.423/152254.601 | 155213.861/151898.401                     | 155212.207/151895.898 | 756                        | 3.0                       | 2.6                                 |
| 89         | SG/APS/B034/26           | Meenamalwaththa<br>Galawudakanda Road                | 155548.83/152342.896                           | 155544.417/152344.581 | 156481.018/152489.773                     | 156485.08/152492.253  | 1680                       | 4.0                       | 3.0                                 |
| 90         | SG/APS/B034/26/01        | Gewaththahena Road<br>First Lane                     | 155812.259/152854.083                          | 155807.217/152852.988 | 155881.989/152886.323                     | 155882.927/152890.212 | 90.69                      | 4.0                       | 3.0                                 |
| 91         | SG/APS/B034/26/02        | Gewaththahena Road<br>Second Lane                    | 156137.361/152707.502                          | 156135.173/152709.799 | 156172.151/152815.675                     | 156169.384/152814.517 | 151.73                     | 3.0                       | 3.0                                 |
| 92         | SG/APS/B034/26/03        | Gewaththahena Road<br>Third Lane                     | 156141.391/152699.11                           | 156145.003/152698.151 | 156061.22/152612.179                      | 156064.117/152612.958 | 148.28                     | 3.0                       | 2.5                                 |
| 93         | SG/APS/B034/27           | Gurukadehena Road                                    | 155206.007/152563.527                          | 155204.082/152567.05  | 155242.19/152686.466                      | 155238.344/152687.568 | 154.24                     | 4.0                       | 3.5                                 |
| 94         | SG/APS/B034/28           | Peellawaththa First Lane                             | 154869.536/152691.801                          | 154873.824/152690.24  | 154751.073/152596.152                     | 154754.425/152598.333 | 221.14                     | 4.0                       | 3.5                                 |
| 95         | SG/APS/B034/29           | Fifth Post Ihala Road                                | 154809.16/152802.307                           | 154805.185/152807.601 | 154907.573/152813.606                     | 154908.043/152817.578 | 124.81                     | 4.0                       | 2.0                                 |
| 96         | SG/APS/B034/30           | Pussalakanda Road                                    | 154427.166/153082.404                          | 154420.883/153083.167 | 155488.137/152921.174                     | 155487.906/152925.667 | 1275.64                    | 4.5                       | 4.0                                 |

| Serial No. | Code of the Road     | Name of the Road                           | Starting Coordinates<br>(Kandawala Sri Lanka ) |                       | Ending Coordinates (Kandawala Sri Lanka ) |                       | Length of the Road (Meter) | Width of the Road (Meter) | Developed Width of the Road (Meter) |
|------------|----------------------|--------------------------------------------|------------------------------------------------|-----------------------|-------------------------------------------|-----------------------|----------------------------|---------------------------|-------------------------------------|
|            |                      |                                            | Left                                           | Right                 | Left                                      | Right                 |                            |                           |                                     |
| 97         | SG/APS/B034/30/01    | Pussalakanda Annasigala Road               | 154792.381/153158.865                          | 154787.287/153159.596 | 154753.1/153504.337                       | 154749.634/153506.333 | 415.23                     | 4.0                       | 3.5                                 |
| 98         | SG/APS/B034/30/01/01 | First Lane of Pussalakanda Annasigala Road | 154742.638/153222.09                           | 154745.056/153218.001 | 154408.76/153347.892                      | 154408.756/153343.891 | 374.39                     | 4.0                       | 3.5                                 |
| 99         | SG/APS/B034/30/02    | Pussalakanda Community Hall Road           | 154998.718/153197                              | 154993.134/153197.319 | 155037.456/153256.341                     | 155035.567/153259.866 | 77.55                      | 4.0                       | 3.5                                 |
| 100        | SG/APS/B034/30/03    | First Lane of Pussalakanda                 | 155179.961/153156.997                          | 155176.157/153158.242 | 155353.978/153314.694                     | 155349.98/153314.623  | 304.23                     | 4.0                       | 3.5                                 |
| 101        | SG/APS/B034/31       | Peellawaththa Road                         | 154406.068/153077.414                          | 154411.176/153077.68  | 154202.873/152646.25                      | 154203.992/152642.41  | 520.81                     | 4.0                       | 3.0                                 |
| 102        | SG/APS/B034/31/01    | Welithotupala Road                         | 154338.58/152979.364                           | 154338.638/152974.272 | 154245.307/153028.339                     | 154245.823/153024.372 | 114.48                     | 4.0                       | 3.0                                 |
| 103        | SG/APS/B034/31/02    | First Lane of Peellawaththa Road           | 154350.511/152910.575                          | 154352.063/152913.891 | 154496.07/152867.97                       | 154498.125/152870.803 | 166.47                     | 3.5                       | 3.0                                 |
| 104        | SG/APS/B034/31/03    | Lindapitiya Road                           | 154304.71/152834.973                           | 154305.897/152837.782 | 154522.292/152705.741                     | 154521.95/152708.722  | 364.55                     | 3.0                       | 2.5                                 |
| 105        | SG/APS/B034/31/03/01 | Lindapitiya Aranya Road                    | 154388.387/152674.926                          | 154392.563/152675.194 | 154550.972/152553.484                     | 154548.342/152555.792 | 236.12                     | 3.5                       | 2.5                                 |
| 106        | SG/APS/B034/31/04    | From Peellawaththa to Gonapenigala Road    | 154275.162/152791.666                          | 154274.09/152788.334  | 154205.965/152809.811                     | 154206.026/152806.312 | 73.42                      | 3.5                       | 3.0                                 |
| 107        | SG/APS/B034/32       | Pimbura Ihawalaththa Footpath              | 154012.825/153424.749                          | 154009.586/153424.804 | 154003.812/153644.448                     | 154001.169/153645.868 | 246.52                     | 3.0                       | 2.0                                 |
| 108        | SG/APS/B034/33       | Ambalanwela Road                           | 153461.878/153590.973                          | 153458.194/153589.411 | 153411.402/153660.025                     | 153410.345/153656.167 | 116.18                     | 4.0                       | 3.5                                 |
| 109        | SG/APS/B034/34       | Gonapenigala Road                          | 153396.573/153201.848                          | 153398.804/153204.009 | 154081.918/152867.054                     | 154082.727/152869.943 | 817.68                     | 3.0                       | 2.5                                 |
| 110        | SG/APS/B034/35       | First Part of Henyaya Road                 | 153389.272/152995.541                          | 153393.184/152998.685 | 153341.616/152602.786                     | 153341.848/152598.292 | 482.11                     | 4.5                       | 4.0                                 |
| 111        | SG/APS/B034/35/01    | Manakanda Road                             | 153430.222/152736.929                          | 153435.079/152739.957 | 154342.32/152408.172                      | 154342.144/152412.168 | 1190.05                    | 4.0                       | 3.5                                 |
| 112        | SG/APS/B034/35/01/01 | First Lane of Manakanda Road               | 153899.665/152576.357                          | 153895.645/152579.514 | 153984.239/152618.235                     | 153981.568/152620.496 | 101.89                     | 3.5                       | 3.0                                 |
| 113        | SG/APS/B034/35/01/02 | Second Lane of Manakanda Road              | 154039.118/152485.79                           | 154036.953/152488.545 | 154106.259/152595.084                     | 154104.673/152598.204 | 134.09                     | 3.5                       | 3.0                                 |
| 114        | SG/APS/B034/35/01/03 | Third Lane of Manakanda Road               | 154041.481/152462.55                           | 154041.738/152459.016 | 153662.298/152526.853                     | 153659.966/152524.243 | 405.75                     | 3.5                       | 3.0                                 |
| 115        | SG/APS/B034/35/01/04 | Fourth Lane of Manakanda Road              | 154126.013/152332.949                          | 154130.983/152333.176 | 154153.784/152303.817                     | 154154.445/152307.255 | 48.53                      | 3.5                       | 3.0                                 |

| Serial No. | Code of the Road  | Name of the Road                             | Starting Coordinates<br>(Kandawala Sri Lanka ) |                       | Ending Coordinates (Kandawala Sri Lanka ) |                       | Length of the Road (Meter) | Width of the Road (Meter) | Developed Width of the Road (Meter) |
|------------|-------------------|----------------------------------------------|------------------------------------------------|-----------------------|-------------------------------------------|-----------------------|----------------------------|---------------------------|-------------------------------------|
|            |                   |                                              | Left                                           | Right                 | Left                                      | Right                 |                            |                           |                                     |
| 116        | SG/APS/B034/35/02 | Kumuruhena Road                              | 153368.378/152619.278                          | 153372.246/152625.574 | 153339.415/151563.978                     | 153342.627/151565.367 | 1204.47                    | 3.5                       | 3.0                                 |
| 117        | SG/APS/B034/36    | Kiwulahena Road                              | 153305.628/153129.141                          | 153306.867/153125.338 | 153206.548/152910.147                     | 153210.448/152911.03  | 285.42                     | 4.0                       | 3.0                                 |
| 118        | SG/APS/B034/37    | Kandaweldola Road                            | 153249.311/153215.57                           | 153252.33/153213.785  | 152981.28/152948.11                       | 152983.391/152943.015 | 423.1                      | 3.5                       | 3.0                                 |
| 119        | SG/APS/B034/38    | From Seventh Post<br>Kandaweldola Road       | 153053.703/153278.299                          | 153056.199/153276.109 | 152948.854/152799.077                     | 152951.034/152796.734 | 1122                       | 3.2                       | 3.0                                 |
| 120        | SG/APS/B034/38/01 | Wedawunhena Road                             | 152713.194/153309.444                          | 152711.435/153304.691 | 152375.237/153406.448                     | 152373.893/153403.216 | 366.85                     | 3.5                       | 3.0                                 |
| 121        | SG/APS/B034/38/02 | Takaranwaththa Road                          | 152680.037/153166.182                          | 152682.453/153163.284 | 152597.369/153144.862                     | 152598.195/153141.461 | 94.28                      | 3.5                       | 3.0                                 |
| 122        | SG/APS/B034/39    | Pimbura Road from<br>Ellakade                | 153159.174/153546.815                          | 153157.519/153553.13  | 153482.772/153802.755                     | 153479.861/153807.714 | 613.27                     | 4.0                       | 3.6                                 |
| 123        | SG/APS/B034/40    | Aluthgewaththe Road                          | 153010.665/153748.025                          | 153009.109/153751.891 | 153219.447/153770.356                     | 153216.519/153773.082 | 268.12                     | 4.0                       | 4.0                                 |
| 124        | SG/APS/B034/41    | Egodawaththa Road                            | 152952.76/153792.175                           | 152954.849/153789.182 | 152590.784/154044.446                     | 152595.397/154047.95  | 764.66                     | 3.5                       | 3.0                                 |
| 125        | SG/APS/B034/42    | Epitawaththa Road                            | 152873.971/153877.869                          | 152877.218/153875.483 | 152835.639/153831.498                     | 152838.333/153828.542 | 65.1                       | 4.0                       | 3.7                                 |
| 126        | SG/APS/B034/43    | Nikagoda Udawaththa<br>Road                  | 152657.431/154083.67                           | 152654.879/154083.362 | 152360.208/154587.182                     | 152360.132/154584.673 | 713.87                     | 2.5                       | 2.0                                 |
| 127        | SG/APS/B034/44    | Nikagoda Udukumbura<br>First Road            | 152348.275/154207.188                          | 152352.569/154205.401 | 152199.322/154093.296                     | 152202.807/154092.968 | 227.71                     | 3.5                       | 2.8                                 |
| 128        | SG/APS/B034/45    | Nikagoda Aludeniya<br>Road                   | 152293.939/154277.524                          | 152292.666/154282.208 | 151888.105/155763.132                     | 151885.466/155765.432 | 1893.83                    | 3.5                       | 3.0                                 |
| 129        | SG/APS/B034/45/01 | Aludeniya<br>Suduwelipotha Road              | 152356.698/154587.11                           | 152356.43/154583.337  | 152159.211/154687.009                     | 152157.809/154683.802 | 265.83                     | 3.5                       | 3.0                                 |
| 130        | SG/APS/B034/45/02 | First Lane of Nikagoda<br>Aludeniya Road     | 151857.452/155248.606                          | 151858.086/155245.608 | 151465.03/155520.798                      | 151466.274/155518.069 | 539.24                     | 3.0                       | 3.0                                 |
| 131        | SG/APS/B034/45/03 | Second Lane of<br>Nikagoda Aludeniya<br>Road | 151863.251/155311.934                          | 151863.102/155316.035 | 152001.775/155288.691                     | 152004.081/155291.959 | 155.73                     | 4.0                       | 3.5                                 |
| 132        | SG/APS/B034/45/04 | Third Lane of Nikagoda<br>Aludeniya          | 151801.975/155463.935                          | 151800.363/155460.522 | 151732.14/155523.606                      | 151729.672/155521.122 | 101.62                     | 3.5                       | 3.0                                 |
| 133        | SG/APS/B034/45/05 | Fourth Lane of<br>Nikagoda Aludeniya<br>Road | 151836.428/155524.305                          | 151834.142/155521.646 | 151834.407/155586.377                     | 151835.461/155589.714 | 117.35                     | 3.5                       | 3.0                                 |
| 134        | SG/APS/B034/46    | Nikagoda Udukumbura<br>Second Road           | 152258.501/154304.292                          | 152263.252/154301.889 | 152204.333/154227.006                     | 152207.714/154227.914 | 141.05                     | 3.5                       | 3.0                                 |

| Serial No. | Code of the Road     | Name of the Road                              | Starting Coordinates<br>(Kandawala Sri Lanka ) |                       | Ending Coordinates (Kandawala Sri Lanka ) |                       | Length of the Road (Meter) | Width of the Road (Meter) | Developed Width of the Road (Meter) |
|------------|----------------------|-----------------------------------------------|------------------------------------------------|-----------------------|-------------------------------------------|-----------------------|----------------------------|---------------------------|-------------------------------------|
|            |                      |                                               | Left                                           | Right                 | Left                                      | Right                 |                            |                           |                                     |
| 135        | SG/APS/B034/47       | Nikagoda Udakumbura Third Road                | 152069.276/154356.638                          | 152072.633/154356.714 | 152142.219/154268.253                     | 152144.721/154269.909 | 121.34                     | 3.0                       | 2.6                                 |
| 136        | SG/APS/B034/48       | First Lane of Nikagoda                        | 151954.285/154343.495                          | 151957.929/154340.37  | 151929.476/154249.566                     | 151930.281/154252.456 | 221.65                     | 3.0                       | 2.5                                 |
| 137        | SG/APS/B034/49       | Akkara 08 Ellakadewaththa Road                | 151611.061/154472.237                          | 151614.777/154471.403 | 151773.68/154023.63                       | 151774.069/154020.655 | 760.82                     | 3.0                       | 3.0                                 |
| 138        | SG/APS/B034/49/01    | Akkara 05 Imbulahithena Road                  | 151938.098/154056.691                          | 151941.446/154057.97  | 151932.947/153924.582                     | 151934.081/153921.271 | 182.92                     | 3.5                       | 3.0                                 |
| 139        | SG/APS/B034/50       | Nikagoda Govipala Road                        | 151211.374/154544.621                          | 151203.484/154546.446 | 151235.423/154749.043                     | 151236.685/154745.247 | 436.11                     | 4.0                       | 3.5                                 |
| 140        | SG/APS/B034/51       | Halgahahena Road                              | 150926.637/154660.74                           | 150923.79/154661.863  | 151152.756/154757.59                      | 151154.921/154759.668 | 334.47                     | 3.0                       | 2.8                                 |
| 141        | SG/APS/B034/52       | Hebbewahena Road                              | 150683.495/154788.477                          | 150679.725/154789.884 | 150827.894/155031.371                     | 150830.496/155033.973 | 730.23                     | 3.7                       | 3.0                                 |
| 142        | SG/APS/B034/52/01    | First Lane of Hebbewahena Road                | 150621.161/155143.169                          | 150617.249/155142.86  | 150647.233/155275.072                     | 150643.57/155274.726  | 137.17                     | 3.7                       | 3.0                                 |
| 143        | SG/APS/B034/52/02    | Second Lane of Hebbewahena Road               | 150789.859/155060.569                          | 150786.209/155063.43  | 150892.89/155196.562                      | 150889.895/155198.701 | 193.95                     | 3.7                       | 3.0                                 |
| 144        | SG/APS/B034/53       | Second Part of Henyaya Road                   | 150599.829/154744.569                          | 150604.025/154746.216 | 151605.162/153221.781                     | 151608.029/153225.251 | 2437.92                    | 4.5                       | 4.0                                 |
| 145        | SG/APS/B034/53/01    | First Lane of Second Part of Henyaya Road     | 150901.005/154361.832                          | 150897.724/154364.184 | 150941.086/154398.682                     | 150937.589/154400.624 | 56.74                      | 4.0                       | 3.7                                 |
| 146        | SG/APS/B034/53/02    | Second Lane of Second Part of Henyaya Road    | 150915.379/154325.617                          | 150916.725/154321.271 | 150779.801/154122.92                      | 150783.759/154123.499 | 277.12                     | 4.0                       | 3.5                                 |
| 147        | SG/APS/B034/53/03    | Third Lane of the Second Part of Henyaya Road | 150956.967/154236.316                          | 150955.374/154240.109 | 151083.371/154306.853                     | 151079.378/154307.09  | 151.05                     | 4.0                       | 3.5                                 |
| 148        | SG/APS/B034/53/04    | Polwaththa Kalugalahenayaya Road              | 151280.724/153714.697                          | 151277.754/153717.657 | 151723.026/153871.479                     | 151724.304/153875.269 | 889.95                     | 4.0                       | 3.6                                 |
| 149        | SG/APS/B034/53/05    | Polwaththa Kosgahahena Road                   | 151285.14/153710.987                           | 151281.635/153713.771 | 151446.688/153665.393                     | 151450.429/153666.811 | 209.62                     | 4.0                       | 3.7                                 |
| 150        | SG/APS/B034/53/06    | Polwaththa Mirishena Road                     | 151566.103/153465.149                          | 151565.211/153468.661 | 152196.977/153652.594                     | 152193.511/153653.566 | 760.52                     | 3.6                       | 3.2                                 |
| 151        | SG/APS/B034/53/06/01 | First Lane of Polwaththa Mirishena Road       | 151726.981/153602.314                          | 151729.907/153603.013 | 151852.779/153438.163                     | 151852.292/153441.124 | 250.01                     | 3.0                       | 3.0                                 |

| Serial No. | Code of the Road              | Name of the Road                                                  | Starting Coordinates<br>(Kandawala Sri Lanka ) |                       | Ending Coordinates (Kandawala Sri Lanka ) |                       | Length of the Road (Meter) | Width of the Road (Meter) | Developed Width of the Road (Meter) |
|------------|-------------------------------|-------------------------------------------------------------------|------------------------------------------------|-----------------------|-------------------------------------------|-----------------------|----------------------------|---------------------------|-------------------------------------|
|            |                               |                                                                   | Left                                           | Right                 | Left                                      | Right                 |                            |                           |                                     |
| 152        | SG/APS/<br>B034/53/06/02      | Second Lane of<br>Polwaththa Mirishena<br>Road                    | 151938.141/153656.04                           | 151942.147/153656.042 | 151937.134/153620.166                     | 151939.911/153623.044 | 37.22                      | 4.0                       | 3.5                                 |
| 153        | SG/APS/<br>B034/53/06/03      | Third Lane of<br>Polwaththa Mirishena<br>Road                     | 151953.98/153659.429                           | 151958.172/153663.244 | 151999.971/153630.358                     | 152002.072/153633.762 | 59.18                      | 4.0                       | 3.5                                 |
| 154        | SG/APS/<br>B034/53/06/04      | Fourth Lane of<br>Polwaththa Mirishena<br>Road                    | 152047.02/153658.921                           | 152043.299/153660.465 | 152055.735/153689.167                     | 152052.301/153687.115 | 37.6                       | 4.0                       | 3.7                                 |
| 155        | SG/APS/B034/53/07             | Polwaththa Temple<br>Road                                         | 151594.161/153234.354                          | 151588.103/153236.539 | 151564.82/153306.85                       | 151560.827/153306.625 | 112.84                     | 4.0                       | 3.5                                 |
| 156        | SG/APS/B034/<br>C404/01       | Ellawita Road                                                     | 160232.449/148423.492                          | 160234.269/148419.848 | 160102.703/148258.795                     | 160106.689/148259.126 | 274.56                     | 4.0                       | 3.5                                 |
| 157        | SG/APS/B034/<br>C404/02       | Road Near Ayagama<br>Pradeshiya Sabha                             | 160277.687/148300.551                          | 160275.962/148303.6   | 160360.472/148318.25                      | 160361.682/148321.535 | 100.54                     | 3.5                       | 2.5                                 |
| 158        | SG/APS/B034/<br>C404/03       | Ayagama Gale Temple<br>Road                                       | 160514.894/147862.732                          | 160512.387/147864.916 | 161099.332/148315.776                     | 161100.116/148318.981 | 1238.54                    | 3.3                       | 3.3                                 |
| 159        | SG/APS/B034/<br>C404/04       | Ayagama<br>Gonapalawaththa Road                                   | 160664.062/147685.186                          | 160661.14/147687.992  | 160692.86/147811.045                      | 160690.171/147809.713 | 165.78                     | 3.0                       | 3.0                                 |
| 160        | SG/APS/B034/<br>C404/05       | Yakahatuwela Pinthenna<br>Road                                    | 160703.313/147661.927                          | 160707.299/147661.312 | 160874.516/146570.34                      | 160876.68/146573.853  | 1755.09                    | 4.0                       | 3.5                                 |
| 161        | SG/APS/B034/<br>C404/05/01    | Witowita Road                                                     | 160882.102/146903.71                           | 160881.546/146904.545 | 160919.215/146948.385                     | 160918.248/146948.684 | 62.65                      | 1.0                       | 1.0                                 |
| 162        | SG/APS/B034/<br>C404/05/02    | First Lane of<br>Yakahatuwela Pinthenna<br>Division A Road        | 160737.493/146781.269                          | 160742.01/146768.491  | 160483.043/146788.777                     | 160479.708/146786.569 | 313.38                     | 4.0                       | 3.5                                 |
| 163        | SG/APS/B034/<br>C404/06       | Amunuowita Road                                                   | 161113.758/147357.258                          | 161115.071/147355.093 | 160997.494/147284.759                     | 160999.217/147282.947 | 172.08                     | 2.5                       | 2.0                                 |
| 164        | SG/APS/B034/<br>C404/07       | Pallekada<br>Liyangahawaththa Road                                | 161319.55/147244.647                           | 161317.94/147247.179  | 161595.737/147295.555                     | 161595.182/147298.504 | 334.92                     | 3.0                       | 3.0                                 |
| 165        | SG/APS/B034/<br>C404/08       | Pallekada<br>Kalatuwakanda Road                                   | 161589.331/146890.54                           | 161590.577/146893.912 | 163580.055/146010.311                     | 163581.573/146013.464 | 2723.02                    | 3.5                       | 3.0                                 |
| 166        | SG/APS/B034/<br>C404/08/01    | First Lane of Pallekada<br>Kalatuwakanda Road                     | 161765.24/146834.981                           | 161762.385/146837.761 | 162260.645/146827.904                     | 162261.944/146831.153 | 592.87                     | 3.5                       | 3.0                                 |
| 167        | SG/APS/B034/<br>C404/08/01/01 | First By Pass of First<br>Lane of Pallekada<br>Kalatuwakanda Road | 161877.614/146942.89                           | 161874.052/146943.326 | 161836.74/147058.352                      | 161834.092/147056.064 | 130.08                     | 3.5                       | 3.0                                 |



| Serial No. | Code of the Road              | Name of the Road                                                   | Starting Coordinates<br>(Kandawala Sri Lanka ) |                       | Ending Coordinates<br>(Kandawala Sri Lanka ) |                       | Length of the<br>Road (Meter) | Width of the Road<br>(Meter) | Developed Width<br>of the Road (Meter) |
|------------|-------------------------------|--------------------------------------------------------------------|------------------------------------------------|-----------------------|----------------------------------------------|-----------------------|-------------------------------|------------------------------|----------------------------------------|
|            |                               |                                                                    | Left                                           | Right                 | Left                                         | Right                 |                               |                              |                                        |
| 168        | SG/APS/B034/<br>C404/08/01/02 | Second By Pass of<br>First Lane of Pallekada<br>Kalatuwakanda Road | 162068.884/146903.431                          | 162064.528/146903.699 | 162065.967/147192.316                        | 162063.483/147189.851 | 363.6                         | 3.5                          | 3.0                                    |
| 169        | SG/APS/B034/<br>C404/08/02    | Second Lane<br>of Pallekada<br>Kalatuwakanda Road                  | 162095.484/146610.42                           | 162092.231/146612.057 | 162075.851/146720.112                        | 162072.543/146718.972 | 159.95                        | 3.5                          | 3.0                                    |
| 170        | SG/APS/B034/<br>C404/08/03    | Third Lane of Pallekada<br>Kalatuwakanda Road                      | 162235.225/146567.227                          | 162231.787/146568.616 | 162277.016/146608.193                        | 162274.259/146609.377 | 67.91                         | 3.0                          | 2.5                                    |
| 171        | SG/APS/B034/<br>C404/08/04    | Fourth Lane<br>of Pallekada<br>Kalatuwakanda Road                  | 162330.51/146539.017                           | 162327.516/146539.222 | 162327.146/146639.195                        | 162324.43/146637.919  | 119.75                        | 3.0                          | 2.5                                    |
| 172        | SG/APS/B034/<br>C404/08/05    | Fifth Lane of Pallekada<br>Kalatuwakanda Road                      | 162878.678/146452.22                           | 162879.894/146456.27  | 162965.425/146459.726                        | 162966.543/146463.043 | 113.09                        | 3.5                          | 3.0                                    |
| 173        | SG/APS/B034/<br>C404/08/06    | Sixth Lane of Pallekada<br>Kalatuwakanda Road                      | 163249.055/146310.42                           | 163251.852/146306.72  | 163186.802/146249.491                        | 163185.128/146245.858 | 101.44                        | 4.0                          | 3.5                                    |
| 174        | SG/APS/B034/<br>C404/08/07    | Seventh Lane<br>of Pallekada<br>Kalatuwakanda Road                 | 163349.292/146179.163                          | 163350.69/146182.28   | 163466.236/146261.559                        | 163469.087/146263.589 | 210.97                        | 3.5                          | 3.0                                    |
| 175        | SG/APS/B034/<br>C404/09       | Pallekade Witowita<br>Road                                         | 161542.933/146841.653                          | 161545.476/146844.786 | 160870.378/146980.519                        | 160869.878/146976.55  | 762.46                        | 4.0                          | 3.0                                    |
| 176        | SG/APS/B034/<br>C404/09/01    | Witowita Batawala<br>Dewala Road                                   | 161530.816/146859.802                          | 161526.513/146860.001 | 161513.995/146908.75                         | 161510.7/146906.482   | 54.77                         | 4.0                          | 3.0                                    |
| 177        | SG/APS/B034/<br>C404/09/02    | First Lane of Pallekada<br>Witowita Road                           | 161244.901/146852.016                          | 161247.853/146851.472 | 161170.512/146835.73                         | 161171.291/146832.833 | 88.88                         | 3.0                          | 3.0                                    |
| 178        | SG/APS/B034/<br>C404/10       | Pallekade<br>Kapugewaththa First<br>Road                           | 161473.741/146680.398                          | 161471.855/146677.447 | 161178.081/146730.885                        | 161181.339/146729.607 | 331.29                        | 3.5                          | 3.0                                    |
| 179        | SG/APS/B034/<br>C404/11       | Pallekade<br>Kapugewaththa Second<br>Road                          | 161465.864/146666.822                          | 161464.162/146663.758 | 161370.433/146707.203                        | 161370.628/146703.708 | 112.86                        | 3.5                          | 3.0                                    |
| 180        | SG/APS/B034/<br>C404/12       | Pallekade<br>Kapugewaththa Third<br>Road                           | 161319.608/146495.3                            | 161318.655/146491.334 | 161145.813/146562.262                        | 161144.251/146558.58  | 192.67                        | 4.0                          | 3.5                                    |
| 181        | SG/APS/B034/<br>C404/13       | Bogahawanguwa By<br>Pass                                           | 160804.117/146384.218                          | 160801.495/146382.584 | 160452.028/146512.394                        | 160453.507/146509.784 | 418.81                        | 3.0                          | 3.0                                    |

| Serial No. | Code of the Road             | Name of the Road                                | Starting Coordinates<br>(Kandawala Sri Lanka ) |                       | Ending Coordinates (Kandawala Sri Lanka ) |                       | Length of the Road (Meter) | Width of the Road (Meter) | Developed Width of the Road (Meter) |
|------------|------------------------------|-------------------------------------------------|------------------------------------------------|-----------------------|-------------------------------------------|-----------------------|----------------------------|---------------------------|-------------------------------------|
|            |                              |                                                 | Left                                           | Right                 | Left                                      | Right                 |                            |                           |                                     |
| 182        | SG/APS/B034/<br>C404/13/01   | First Lane of Bogahawela                        | 160714.613/146378.184                          | 160717.357/146376.873 | 160680.716/146305.937                     | 160683.448/146304.696 | 81.59                      | 3.0                       | 3.0                                 |
| 183        | SG/APS/B034/<br>C404/13/02   | Second Lane of Bogahawela                       | 160663.341/146420.705                          | 160665.793/146418.821 | 160614.46/146365.428                      | 160615.045/146362.485 | 80.35                      | 3.0                       | 3.0                                 |
| 184        | SG/APS/B034/<br>C404/14      | Pitakanda Oluwilakanda Road                     | 160597.821/145684.591                          | 160599.598/145687.607 | 160793.718/145549.191                     | 160795.465/145552.225 | 245.86                     | 3.5                       | 2.7                                 |
| 185        | SG/APS/B034/<br>C404/15      | Pitakanda Malgahahena Road                      | 160800.708/145218.773                          | 160803.44/145216.441  | 160467.232/143887.714                     | 160470.507/143889.052 | 1695.47                    | 3.5                       | 2.5                                 |
| 186        | SG/APS/B034/<br>C404/15/01   | First Lane of Pitakanda Malgahahena             | 160667.954/144809.794                          | 160667.565/144806.819 | 160250.128/145116.823                     | 160248.197/145114.528 | 554.23                     | 3.0                       | 3.0                                 |
| 187        | SG/APS/B034/<br>C404/16      | First Lane of Gawaragiriya                      | 161128.747/144589.87                           | 161128.216/144586.652 | 161049.572/144682.218                     | 161046.572/144682.209 | 147.67                     | 3.0                       | 3.0                                 |
| 188        | SG/APS/B034/<br>C404/17      | Second Lane of Gawaragiriya                     | 161135.292/144579.446                          | 161135.64/144582.433  | 161180.913/144512.54                      | 161182.41/144515.14   | 130.99                     | 3.0                       | 3.0                                 |
| 189        | SG/APS/B034/<br>C404/18      | Third Lane of Gawaragiriya                      | 161127.88/144464.7                             | 161127.449/144461.227 | 161062.547/144493.465                     | 161062.922/144489.985 | 77.67                      | 3.5                       | 3.0                                 |
| 190        | SG/APS/B034/<br>C404/19      | Gawaragiriya Raigamkanda Dumbaramana Road       | 161779.411/143034.835                          | 161779.803/143040.087 | 164105/141682.101                         | 164098.104/141693.573 | 2827.95                    | 5.0                       | 2.8                                 |
| 191        | SG/APS/B034/<br>C404/19/01   | First Lane of Raigamkanda                       | 162472.51/142538.194                           | 162477.055/142538.346 | 162926.879/142179.351                     | 162924.239/142181.648 | 598.79                     | 3.5                       | 2.5                                 |
| 192        | SG/APS/B034/<br>C404/20      | Wathukaragama Puwakwaththa Road                 | 161830.697/142377.098                          | 161831.329/142372.877 | 161658.235/142284.563                     | 161660.779/142281.477 | 200.13                     | 4.0                       | 2.5                                 |
| 193        | SG/APS/B034/<br>C404/20/01   | Wathukaragama Galwaththa Road                   | 161770.912/142351.185                          | 161767.49/142348.967  | 161407.504/142626.852                     | 161406.567/142622.963 | 484.68                     | 4.0                       | 2.5                                 |
| 194        | SG/APS/B034/<br>C404/21      | Wathukaragama Egirikanaththa Road               | 161854.188/142336.153                          | 161857.671/142334.179 | 162065.157/142085.338                     | 162069.155/142085.488 | 465.95                     | 4.0                       | 2.5                                 |
| 195        | SG/APS/B034/<br>C404/21/01   | First Lane of Wathukaragama Egirikanaththa Road | 161853.994/142265.949                          | 161857.565/142259.677 | 161772.003/142238.716                     | 161770.111/142236.387 | 210.73                     | 3.0                       | 2.5                                 |
| 196        | SG/APS/B034/<br>C404/22      | Wathukaragama Dorlapitiya Road                  | 162332.269/142015.546                          | 162336.192/142013.515 | 162224.993/141974.511                     | 162227.987/141971.858 | 124.22                     | 4.0                       | 3.0                                 |
| 197        | SG/APS/B034/<br>C404/D405/01 | Pallekada Welikadawaththa Road                  | 161844.513/146592.528                          | 161847.643/146590.71  | 161750.31/146468.354                      | 161753.01/146467.049  | 233.54                     | 3.0                       | 2.0                                 |

| Serial No. | Code of the Road                       | Name of the Road                                      | Starting Coordinates<br>(Kandawala Sri Lanka ) |                       | Ending Coordinates<br>(Kandawala Sri Lanka ) |                       | Length of the Road<br>(Meter) | Width of the Road<br>(Meter) | Developed Width<br>of the Road (Meter) |
|------------|----------------------------------------|-------------------------------------------------------|------------------------------------------------|-----------------------|----------------------------------------------|-----------------------|-------------------------------|------------------------------|----------------------------------------|
|            |                                        |                                                       | Left                                           | Right                 | Left                                         | Right                 |                               |                              |                                        |
| 198        | SG/APS/B034/<br>C404/D405/02           | First Lane of Pallekada<br>Gamikkanda                 | 162037.316/146402.471                          | 162040.726/146400.334 | 162174.399/145975.895                        | 162175.937/145979.587 | 563.2                         | 4.0                          | 2.7                                    |
| 199        | SG/APS/B034/<br>C404/D405/03           | Second Lane of<br>Pallekada Gamikkanda                | 162453.292/146174.872                          | 162456.176/146173.464 | 162428.868/145826.889                        | 162431.61/145825.195  | 399.09                        | 3.0                          | 2.5                                    |
| 200        | SG/APS/B034/<br>C404/D405/04           | First Lane of Pallekada<br>Kalatuwakanda              | 162474.041/146170.034                          | 162470.718/146171.919 | 162504.53/146482.959                         | 162500.934/146484.458 | 488.03                        | 3.8                          | 3.0                                    |
| 201        | SG/APS/B034/<br>C404/D405/05           | Second Lane<br>Footpath of Pallekada<br>Kalatuwakanda | 162686.261/146095.816                          | 162683.748/146096.055 | 162811.398/146422.064                        | 162808.898/146422.148 | 478.88                        | 2.5                          | 1.0                                    |
| 202        | SG/APS/B034/<br>C404/D405/06           | Gangodakanda<br>Melgodella Road                       | 162968.06/145953.49                            | 162965.454/145954.98  | 163006.478/146187.935                        | 163003.508/146188.359 | 262.04                        | 3.0                          | 2.6                                    |
| 203        | SG/APS/B034/<br>C404/D405/07           | Gangodakanda Akkara<br>60 Kalatuwakanda Road          | 163512.077/145858.981                          | 163508.787/145861.253 | 163471.577/146000.074                        | 163469.503/145995.972 | 176.79                        | 3.0                          | 2.0                                    |
| 204        | SG/APS/B034/<br>C404/D405/08           | Watakurugala Road                                     | 163588.386/145811.609                          | 163591.924/145808.958 | 164489.39/144732.269                         | 164490.466/144736.122 | 1968.75                       | 4.0                          | 3.3                                    |
| 205        | SG/APS/B034/<br>C404/D405/08/01        | Watakurugala Henyaya<br>Road                          | 163566.841/145755.912                          | 163568.726/145759.463 | 163965.736/145418.686                        | 163968.755/145414.624 | 645.72                        | 4.0                          | 3.5                                    |
| 206        | SG/APS/B034/<br>C404/D405/08/02        | Ellawita Henyaya Road                                 | 163496.965/145572.992                          | 163499.761/145569.916 | 163253.998/145287.284                        | 163257.699/145288.802 | 628.02                        | 4.0                          | 3.5                                    |
| 207        | SG/APS/B034/<br>C404/D405/08/03        | Ketakerella Henyaya<br>Road                           | 163616.035/145268.563                          | 163613.876/145271.966 | 164357.348/145066.841                        | 164354.49/145069.726  | 961.49                        | 4.0                          | 3.5                                    |
| 208        | SG/APS/<br>B034/C404/<br>D405/08/03/01 | Henyaya Ketakerella<br>Pahala Road                    | 163990.074/145237.543                          | 163987.423/145240.036 | 163851.196/145487.983                        | 163851.066/145484.486 | 364.15                        | 3.5                          | 2.5                                    |
| 209        | SG/APS/B034/<br>C404/D405/09           | Akkara 36 First Lane                                  | 163800.119/145712.003                          | 163797.125/145714.771 | 164706.8/145736.521                          | 164709.94/145738.999  | 1311.94                       | 4.0                          | 3.5                                    |
| 210        | SG/APS/B034/<br>C404/D405/10           | Akkara 36 Second Lane                                 | 164021.24/145639.8                             | 164017.23/145641.462  | 163951.793/145849.01                         | 163947.772/145849.286 | 415.39                        | 4.0                          | 3.5                                    |
| 211        | SG/APS/B034/<br>C404/D405/11           | Baduwalakanda<br>Galkerekanda Road                    | 165014.641/145280.167                          | 165015.231/145284.137 | 165346.832/145401.242                        | 165346.488/145405.227 | 431.27                        | 4.0                          | 3.5                                    |
| 212        | SG/APS/B034/<br>C404/D405/11/01        | Galkerekanda Galathura<br>Road                        | 165158.3/145353.973                            | 165152.821/145351.331 | 166198.582/145939.273                        | 166195.509/145937.524 | 1493.54                       | 3.0                          | 2.5                                    |
| 213        | SG/APS/B034/<br>C404/D405/12           | Baduwalakanda Akkara<br>100 By Pass                   | 165015.18/145244.641                           | 165017.981/145242.209 | 165068.311/145044.802                        | 165069.977/145046.032 | 223.49                        | 2.0                          | 1.0                                    |

| Serial No. | Code of the Road                       | Name of the Road                                                                | Starting Coordinates<br>(Kandawala Sri Lanka ) |                       | Ending Coordinates (Kandawala Sri Lanka ) |                       | Length of the Road (Meter) | Width of the Road (Meter) | Developed Width of the Road (Meter) |
|------------|----------------------------------------|---------------------------------------------------------------------------------|------------------------------------------------|-----------------------|-------------------------------------------|-----------------------|----------------------------|---------------------------|-------------------------------------|
|            |                                        |                                                                                 | Left                                           | Right                 | Left                                      | Right                 |                            |                           |                                     |
| 214        | SG/APS/B034/<br>C404/D408/01           | Labuelahena Road                                                                | 160521.458/145830.534                          | 160525.82/145828.924  | 160432.723/145663.672                     | 160436.722/145663.788 | 281.21                     | 4.0                       | 3.5                                 |
| 215        | SG/APS/B034/<br>C404/D408/02           | Tea Colony<br>Mahindaramaya Road                                                | 160446.711/145882.744                          | 160442.926/145885.192 | 160619.012/146203.898                     | 160615.756/146202.615 | 457.76                     | 3.5                       | 3.0                                 |
| 216        | SG/APS/B034/<br>C404/D408/02/01        | First Lane of Tea Colony<br>Mahindaramaya Road                                  | 160442.851/145922.735                          | 160442.156/145926.425 | 160483.797/145913.543                     | 160481.311/145916.511 | 47.94                      | 3.5                       | 3.0                                 |
| 217        | SG/APS/B034/<br>C404/D408/02/02        | Second Lane of Tea<br>Colony Mahindaramaya<br>Road                              | 160436.421/145971.767                          | 160435.934/145975.38  | 160544.63/145900.79                       | 160546.658/145903.644 | 169.64                     | 3.5                       | 3.0                                 |
| 218        | SG/APS/<br>B034/C404/<br>D408/02/02/01 | First By Pass of Second<br>Lane of Tea Colony<br>Mahindaramaya Road             | 160483.556/145920.016                          | 160481.336/145924.6   | 160511.205/145979.264                     | 160508.558/145977.853 | 77.25                      | 3.0                       | 2.0                                 |
| 219        | SG/APS/B034/<br>C404/D408/02/03        | Third Lane of Tea<br>Colony Mahindaramaya<br>Road                               | 160497.179/146104.457                          | 160502.297/146106.814 | 160622.966/146038.814                     | 160623.854/146042.199 | 157.01                     | 3.5                       | 3.0                                 |
| 220        | SG/APS/B034/<br>C404/D408/02/04        | Fourth of Tea Colony<br>Mahindaramaya Road                                      | 160613.368/146186.927                          | 160617.507/146187.826 | 160787.105/146149.908                     | 160786.575/146153.368 | 189.6                      | 3.5                       | 3.0                                 |
| 221        | SG/APS/B034/<br>C404/D408/03           | Mahindaramaya First<br>Lane                                                     | 160355.127/146027.079                          | 160352.312/146029.781 | 160402.833/146058.487                     | 160403.62/146061.383  | 77.36                      | 3.0                       | 3.0                                 |
| 222        | SG/APS/B034/<br>C404/D408/04           | Hewaheta Samagi<br>Mawatha                                                      | 160333.715/146026.165                          | 160330.912/146023.308 | 159539.665/146365.582                     | 159545.419/146358.971 | 1699.38                    | 4.0                       | 3.0                                 |
| 223        | SG/APS/B034/<br>C404/D408/04/01        | First Lane of Hewaheta<br>Samagi Mawatha                                        | 159844.226/146691.312                          | 159841.171/146691.491 | 160035.912/146800.095                     | 160032.973/146800.693 | 280.25                     | 3.0                       | 2.5                                 |
| 224        | SG/APS/<br>B034/C404/<br>D408/04/01/01 | First By Pass of First<br>Lane of Samagi<br>Mawatha                             | 159861.741/146731.182                          | 159857.518/146729.35  | 159889.727/146770.212                     | 159887.787/146770.695 | 54.14                      | 2.0                       | 2.0                                 |
| 225        | SG/APS/B034/<br>C404/D408/04/02        | Second Lane of<br>Hewaheta Samagi<br>Mawatha                                    | 159728.552/146728.858                          | 159724.349/146728.619 | 159621.929/146975.422                     | 159618.476/146973.403 | 477.04                     | 4.0                       | 3.0                                 |
| 226        | SG/APS/<br>B034/C404/<br>D408/04/02/01 | Footpath - First By Pass<br>Way of Second Lane<br>of Hewaheta Samagi<br>Mawatha | 159684.662/146936.945                          | 159685.741/146936.62  | 159659.818/146854.201                     | 159660.429/146853.41  | 114.3                      | 1.0                       | 1.0                                 |
| 227        | SG/APS/B034/<br>C404/D408/04/03        | Nayadegala Temple<br>Road                                                       | 159527.537/146619.396                          | 159528.152/146616.423 | 159454.032/146835.225                     | 159452.04/146837.468  | 272.6                      | 3.0                       | 3.0                                 |

| Serial No. | Code of the Road                       | Name of the Road                               | Starting Coordinates<br>(Kandawala Sri Lanka ) |                       | Ending Coordinates<br>(Kandawala Sri Lanka ) |                       | Length of the<br>Road (Meter) | Width of the Road<br>(Meter) | Developed Width<br>of the Road (Meter) |
|------------|----------------------------------------|------------------------------------------------|------------------------------------------------|-----------------------|----------------------------------------------|-----------------------|-------------------------------|------------------------------|----------------------------------------|
|            |                                        |                                                | Left                                           | Right                 | Left                                         | Right                 |                               |                              |                                        |
| 228        | SG/APS/B034/<br>C404/D408/05           | Tea Colony Manel<br>Mawatha                    | 160127.361/145996.403                          | 160136.435/145993.731 | 159972.445/145325.07                         | 159976.308/145326.109 | 1066.31                       | 4.0                          | 3.0                                    |
| 229        | SG/APS/B034/<br>C404/D408/06           | First Lane of Pitakanda<br>Tea Colony Road     | 159935.545/146138.611                          | 159931.765/146137.118 | 160021.294/146332.061                        | 160017.931/146334.367 | 237.03                        | 4.0                          | 3.0                                    |
| 230        | SG/APS/B034/<br>C404/D408/07           | Second Lane of<br>Pitakanda Tea Colony<br>Road | 159904.209/146054.641                          | 159908.641/146056.417 | 159969.111/146013.315                        | 159972.1/146015.971   | 80.33                         | 4.0                          | 3.0                                    |
| 231        | SG/APS/B034/<br>C404/D408/08           | Peragahawanguwa Inner<br>Road                  | 159857.111/146242.784                          | 159853.795/146244.029 | 159711.282/146499.991                        | 159709.728/146496.855 | 358.11                        | 3.5                          | 2.5                                    |
| 232        | SG/APS/B034/<br>C404/D408/09           | Tea Colony<br>Divigalpoththa Road              | 159460.488/146382.954                          | 159464.417/146384.485 | 159785.131/145677.525                        | 159788.05/145679.456  | 987.55                        | 3.5                          | 2.5                                    |
| 233        | SG/APS/B034/<br>C404/D408/10           | Tea Colony Batahena<br>Road                    | 159381.228/146257.082                          | 159383.543/146259.709 | 158653.716/145864.021                        | 158653.703/145860.52  | 1088                          | 3.5                          | 2.5                                    |
| 234        | SG/APS/B034/<br>C404/D408/10/01        | First Lane of Tea Colony<br>Batahena Road      | 159023.381/145826.412                          | 159026.802/145825.655 | 159031.943/145705.343                        | 159035.056/145703.743 | 128.99                        | 3.5                          | 2.5                                    |
| 235        | SG/APS/B034/<br>C404/D408/10/02        | Batahena<br>Gangabadathenna Road               | 158823.117/145833.604                          | 158827.38/145833.628  | 157898.987/146369.526                        | 157897.891/146365.679 | 1281.97                       | 4.0                          | 2.5                                    |
| 236        | SG/APS/<br>B034/C404/<br>D408/10/02/01 | First Lane of Batahena<br>Gangabadathenna Road | 158123.941/146033.877                          | 158126.979/146032.992 | 158118.056/145966                            | 158120.711/145967.398 | 71.9                          | 3.0                          | 2.5                                    |
| 237        | SG/APS/B034/<br>C404/D408/10/03        | Batahena Panwilathenna<br>Road                 | 158665.833/145861.996                          | 158662.019/145863.469 | 158452.434/146279.232                        | 158454.773/146275.988 | 640.35                        | 4.0                          | 3.0                                    |
| 238        | SG/APS/B034/<br>C404/D408/11           | Tea Colony Namandiya<br>Road                   | 159260.484/146291.527                          | 159260.331/146287.138 | 159027.237/146166.165                        | 159026.768/146162.697 | 348.73                        | 3.5                          | 2.5                                    |
| 239        | SG/APS/B034/<br>C404/D408/12           | Kanduruwandola<br>Galapalla Road               | 159290.047/146758.405                          | 159287.228/146760.688 | 160057.767/147501.851                        | 160054.738/147503.62  | 1411.76                       | 3.5                          | 2.5                                    |
| 240        | SG/APS/B034/<br>C404/D408/13           | Pitakanda<br>Thembugalpothhta<br>Gamsabha Road | 158992.757/146918.043                          | 158988.008/146924.988 | 159832.598/147571.895                        | 159828.886/147573.398 | 1487.5                        | 4.0                          | 2.0                                    |
| 241        | SG/APS/B034/<br>C404/D408/14           | Pitakanda Thalpathgala<br>Gendagala Road       | 158955.393/146975.354                          | 158951.401/146974.973 | 156821.817/149321.023                        | 156824.14/149317.398  | 4026.87                       | 4.0                          | 2.8                                    |
| 242        | SG/APS/B034/<br>C404/D408/14/01        | Pitakanda Thalpathgala<br>Road                 | 158841.061/147045.431                          | 158837.28/147049.861  | 158171.437/147818.672                        | 158172.122/147814.73  | 1444.73                       | 4.0                          | 2.5                                    |
| 243        | SG/APS/B034/<br>C404/D408/14/02        | First Lane of Pitakanda<br>Thalpathgala Road   | 157498.96/147878.859                           | 157499.586/147874.677 | 157234.824/148089.31                         | 157231.423/148087.205 | 361.03                        | 4.0                          | 2.5                                    |

| Serial No. | Code of the Road                       | Name of the Road                                               | Starting Coordinates<br>(Kandawala Sri Lanka ) |                       | Ending Coordinates (Kandawala Sri Lanka ) |                       | Length of the Road (Meter) | Width of the Road (Meter) | Developed Width of the Road (Meter) |
|------------|----------------------------------------|----------------------------------------------------------------|------------------------------------------------|-----------------------|-------------------------------------------|-----------------------|----------------------------|---------------------------|-------------------------------------|
|            |                                        |                                                                | Left                                           | Right                 | Left                                      | Right                 |                            |                           |                                     |
| 244        | SG/APS/B034/<br>C404/D408/15           | Pitakanda First Lane -<br>Footpath                             | 158952.29/146786.431                           | 158950.896/146783.128 | 158653.804/146783.737                     | 158655.668/146779.791 | 330.99                     | 3.0                       | 2.6                                 |
| 245        | SG/APS/B034/<br>C404/D408/16           | Pitakanda<br>Panwilathenna Road                                | 158992.752/146695.263                          | 158995.733/146698.178 | 158585.268/146197.093                     | 158584.856/146193.067 | 839.02                     | 4.0                       | 3.0                                 |
| 246        | SG/APS/B034/<br>C404/D408/17           | Second Lane of<br>Pitakanda Road                               | 158938.103/146697.138                          | 158942.203/146696.806 | 158961.325/146672.98                      | 158964.134/146674.035 | 36.88                      | 3.0                       | 2.6                                 |
| 247        | SG/APS/B034/<br>C404/D408/18           | Third Lane of Pitakanda<br>Road                                | 158527.876/146838.288                          | 158530.889/146838.527 | 158516.682/146572.202                     | 158517.281/146575.142 | 301.63                     | 3.0                       | 2.5                                 |
| 248        | SG/APS/B034/<br>C404/D408/19           | Fourth Lane of<br>Pitakanda Road                               | 158391.624/146794.043                          | 158394.664/146793.94  | 158383.118/146734.843                     | 158383.936/146731.956 | 68.16                      | 3.0                       | 2.6                                 |
| 249        | SG/APS/B034/<br>C404/D408/20           | Fifth Lane of Pitakanda<br>Road                                | 158371.028/146839.404                          | 158370.205/146841.229 | 158389.514/146863.734                     | 158387.878/146864.886 | 33.99                      | 2.0                       | 1.6                                 |
| 250        | SG/APS/B034/<br>C404/D408/21           | Sixth Lane of Pitakanda<br>Road                                | 158320.446/146865.636                          | 158314.122/146867.684 | 157949.878/146559.532                     | 157951.843/146556.634 | 1178.49                    | 3.5                       | 3.0                                 |
| 251        | SG/APS/B034/<br>C404/D408/21/01        | First By Pass - Footpath<br>of Sixth Lane of<br>Pitakanda Road | 157801.663/147049.828                          | 157798.386/147047.874 | 157712.911/147152.417                     | 157710.026/147153.239 | 165.53                     | 3.0                       | 2.5                                 |
| 252        | SG/APS/B034/<br>C404/D408/22           | Pitakanda Gamsabha<br>Footpath                                 | 158185.44/146770.019                           | 158188.761/146770.059 | 157934.147/146347.428                     | 157935.373/146343.932 | 545.86                     | 3.0                       | 1.6                                 |
| 253        | SG/APS/B034/<br>C404/D408/23           | Seventh Lane of<br>Pitakanda Road                              | 158184.025/146774.431                          | 158185.44/146770.019  | 157856.121/146923.467                     | 157860.114/146923.231 | 434.81                     | 4.0                       | 1.0                                 |
| 254        | SG/APS/B034/<br>C404/D406/01           | Ambagaha Junction<br>Kalumediya Road                           | 161131.443/145171.071                          | 161134.896/145173.252 | 162750.019/144418.317                     | 162752.289/144421.611 | 2582.81                    | 4.0                       | 3.0                                 |
| 255        | SG/APS/B034/<br>C404/D406/01/01        | First Lane of<br>Kalumediya Road                               | 162224.666/144453.272                          | 162227.802/144450.355 | 162240.579/144363.174                     | 162241.403/144366.058 | 103.38                     | 3.0                       | 2.5                                 |
| 256        | SG/APS/B034/<br>C404/D406/01/02        | Kaludiya Thekanda<br>Kuttikanda Road                           | 162264.039/144484.394                          | 162260.383/144487.966 | 164605.873/142928.664                     | 164610.047/142928.024 | 3867.5                     | 4.0                       | 3.0                                 |
| 257        | SG/APS/<br>B034/C404/<br>D406/01/02/01 | First Lane of Kaludiya<br>Thekanda Kuttikanda<br>Road          | 164581.481/143010.128                          | 164579.459/143013.662 | 164648.764/143122.174                     | 164646.671/143125.582 | 137.74                     | 4.0                       | 3.0                                 |
| 258        | SG/APS/B034/<br>C404/D406/01/03        | Second Lane of<br>Kalumediya Road                              | 162112.541/144752.893                          | 162110.722/144749.256 | 161559.35/145069.992                      | 161557.014/145066.745 | 667.89                     | 4.0                       | 3.5                                 |
| 259        | SG/APS/B034/<br>C404/D406/01/04        | Third Lane of<br>Kalumediya Road                               | 162123.865/144753.511                          | 162126.766/144755.492 | 162212.608/144716.623                     | 162213.008/144720.099 | 99.83                      | 3.5                       | 3.0                                 |

| Serial No. | Code of the Road                | Name of the Road                                   | Starting Coordinates<br>(Kandawala Sri Lanka ) |                       | Ending Coordinates<br>(Kandawala Sri Lanka ) |                       | Length of the<br>Road (Meter) | Width of the Road<br>(Meter) | Developed Width<br>of the Road (Meter) |
|------------|---------------------------------|----------------------------------------------------|------------------------------------------------|-----------------------|----------------------------------------------|-----------------------|-------------------------------|------------------------------|----------------------------------------|
|            |                                 |                                                    | Left                                           | Right                 | Left                                         | Right                 |                               |                              |                                        |
| 260        | SG/APS/B034/<br>C404/D406/01/05 | Fourth Lane of<br>Kalumediya Road                  | 162370.841/144695.009                          | 162366.643/144697.738 | 162578.124/144642.282                        | 162581.031/144644.23  | 244.7                         | 3.5                          | 3.0                                    |
| 261        | SG/APS/B034/<br>C404/D406/02    | Ambagaha Junction<br>Gamsabha Road                 | 161135.019/145178.676                          | 161132.62/145175.212  | 161022.205/145644.805                        | 161019.354/145641.999 | 557.3                         | 4.0                          | 2.5                                    |
| 262        | SG/APS/B034/<br>C404/D406/03    | Heressa<br>Gamikkandawaththa<br>Road               | 161605.18/145371.611                           | 161608.64/145371.892  | 162768.247/144927.2                          | 162765.285/144927.678 | 1417.51                       | 3.0                          | 2.5                                    |
| 263        | SG/APS/B034/<br>C404/D406/03/01 | First Lane of Heressa<br>Gamikkandawaththa<br>Road | 161723.374/145276.48                           | 161725.7/145273.754   | 161612.773/145238.659                        | 161612.75/145235.159  | 125.73                        | 3.5                          | 3.0                                    |
| 264        | SG/APS/B034/<br>C404/D406/03/02 | Heressa<br>Gamikkandawaththa<br>Kalumediya Road    | 162368.317/144896.297                          | 162375.609/144893.679 | 162499.257/144666.71                         | 162502.681/144664.757 | 298.32                        | 3.5                          | 2.0                                    |
| 265        | SG/APS/B034/<br>C404/D406/04    | First Lane of Diggala<br>Heressa                   | 161757.972/145517.095                          | 161753.657/145517.637 | 161631.558/145673.812                        | 161634.352/145672.721 | 324.09                        | 3.0                          | 2.5                                    |
| 266        | SG/APS/B034/<br>C404/D406/05    | Second Lane of Diggala<br>Heressa                  | 161830.27/145488.7                             | 161827.098/145490.218 | 161859.82/145549.14                          | 161857.127/145551.377 | 70.26                         | 3.5                          | 3.0                                    |
| 267        | SG/APS/B034/<br>C404/D406/06    | Third Lane Diggala<br>Heressa                      | 162188.258/145563.453                          | 162185.755/145561.775 | 161942.929/145692.707                        | 161939.989/145693.305 | 307                           | 3.0                          | 2.5                                    |
| 268        | SG/APS/B034/<br>C404/D406/07    | Gamikkanada Pallekada<br>Road                      | 162742.986/145275.341                          | 162740.918/145278.928 | 162286.339/145870.993                        | 162287.869/145867.297 | 976.53                        | 4.0                          | 3.0                                    |
| 269        | SG/APS/B034/<br>C404/D406/07/01 | First Lane of<br>Gamikkanda Pallekada              | 162807.26/145344.143                           | 162810.308/145346.885 | 162934.139/145311.753                        | 162930.158/145312.137 | 163.63                        | 4.0                          | 2.5                                    |
| 270        | SG/APS/B034/<br>C404/D406/08    | Heressa Akkara 20 Road                             | 162781.233/145178.911                          | 162783.57/145175.794  | 163371.974/144353.077                        | 163372.966/144350.245 | 1227.93                       | 3.0                          | 2.5                                    |
| 271        | SG/APS/B034/<br>C404/D406/08/01 | Haressa Akkara 20<br>Galpoththa Road               | 163169.07/144636.912                           | 163172.194/144635.587 | 163154.466/144365.837                        | 163156.867/144367.636 | 449.28                        | 3.0                          | 2.5                                    |
| 272        | SG/APS/B034/<br>C404/D406/09    | Diggala Heressa Road                               | 162982.034/145043.287                          | 162978.825/145045.674 | 163923.35/144979.121                         | 163920.473/144982.068 | 1085.36                       | 4.0                          | 3.0                                    |
| 273        | SG/APS/B034/<br>C404/D406/09/01 | Diggala Mukalana Road                              | 163169.314/145100.199                          | 163169.314/145100.199 | 163056.984/145390.869                        | 163054.742/145388.875 | 379.65                        | 3.0                          | 2.0                                    |
| 274        | SG/APS/B034/<br>C404/D406/10    | Diggala Heressa Fourth<br>Lane                     | 163495.456/144665.743                          | 163490.517/144667.758 | 163580.059/144758.336                        | 163580.113/144761.836 | 232.18                        | 3.5                          | 2.5                                    |
| 275        | SG/APS/B034/<br>C404/D406/11    | Diggala Heressa By<br>Pass-Footpath                | 163662.368/144590.539                          | 163660.819/144591.402 | 163837.071/144889.362                        | 163836.118/144888.003 | 405.69                        | 1.5                          | 1.0                                    |



| Serial No. | Code of the Road                       | Name of the Road                                            | Starting Coordinates<br>(Kandawala Sri Lanka ) |                       | Ending Coordinates (Kandawala Sri Lanka ) |                       | Length of the Road (Meter) | Width of the Road (Meter) | Developed Width of the Road (Meter) |
|------------|----------------------------------------|-------------------------------------------------------------|------------------------------------------------|-----------------------|-------------------------------------------|-----------------------|----------------------------|---------------------------|-------------------------------------|
|            |                                        |                                                             | Left                                           | Right                 | Left                                      | Right                 |                            |                           |                                     |
| 276        | SG/APS/B034/<br>C404/D406/12           | Kuttikanda Road                                             | 163664.449/144585.944                          | 163667.172/144584.426 | 164044.067/144246.188                     | 164044.113/144249.187 | 806.19                     | 3.0                       | 3.0                                 |
| 277        | SG/APS/B034/<br>C404/D406/12/01        | Kuttikanda Umandola Road                                    | 163639.496/144482.403                          | 163639.278/144479.904 | 163494.483/144343.5                       | 163496.523/144344.945 | 256.78                     | 2.5                       | 2.0                                 |
| 278        | SG/APS/B034/<br>C404/D407/01           | First Lane of Munihinkanda Road of Gawaragiriya Welamandiya | 160699.858/143935.506                          | 160703.361/143935.567 | 160661.878/143848.602                     | 160664.132/143845.925 | 105.65                     | 3.5                       | 3.0                                 |
| 279        | SG/APS/B034/<br>C404/D407/02           | Gawaragiriya Kolambewa Road                                 | 160327.199/143850.242                          | 160329.754/143845.734 | 158174.679/143543.167                     | 158176.11/143540.53   | 4713.83                    | 3.0                       | 2.8                                 |
| 280        | SG/APS/B034/<br>C404/D407/02/01        | First Lane of Gamwasama                                     | 160148.25/143158.168                           | 160149.739/143161.848 | 160251.028/143076.245                     | 160254.979/143076.863 | 140.62                     | 4.0                       | 3.0                                 |
| 281        | SG/APS/B034/<br>C404/D407/02/02        | Nebadakanda Road                                            | 159992.397/143096.675                          | 159988.046/143097.569 | 158432.198/143398.985                     | 158433.316/143395.136 | 2083.16                    | 4.0                       | 3.0                                 |
| 282        | SG/APS/<br>B034/C404/<br>D407/02/02/01 | Kondagala Road                                              | 158669.768/143759.738                          | 158673.128/143762.179 | 158169.001/143726.865                     | 158173.893/143724.586 | 1119.83                    | 4.0                       | 3.0                                 |
| 283        | SG/APS/<br>B034/C404/<br>D407/02/02/02 | First Lane of Nebadakanda Road                              | 158454.333/143404.292                          | 158459.596/143408.227 | 158565.735/143409.54                      | 158564.696/143413.403 | 113.2                      | 4.0                       | 3.0                                 |
| 284        | SG/APS/B034/<br>C404/D407/02/03        | Niggaha Bulathsinhala Road                                  | 159860.232/142810.67                           | 159869.03/142810.453  | 160719.397/142209.444                     | 160720.446/142213.304 | 1113.02                    | 4.0                       | 3.0                                 |
| 285        | SG/APS/<br>B034/C404/<br>D407/02/03/01 | First Lane of Niggaha Bulathsinhala Road                    | 160588.267/142272.567                          | 160586.011/142274.583 | 160721.102/142641.984                     | 160721.439/142644.966 | 924.49                     | 3.0                       | 2.6                                 |
| 286        | SG/APS/B034/<br>C404/D407/02/04        | Gamwasama Bodhiya Nebadakanda Road                          | 159758.823/142781.741                          | 159754.918/142780.886 | 159730.077/143276.113                     | 159727.642/143278.002 | 1077.1                     | 3.0                       | 3.0                                 |
| 287        | SG/APS/B034/<br>C404/D407/02/05        | First Lane of Gawaragiriya Kolambewa Road                   | 159720.815/142722.739                          | 159720.174/142719.347 | 159357.438/142973.765                     | 159359.763/142971.87  | 515.98                     | 3.0                       | 2.7                                 |
| 288        | SG/APS/B034/<br>C404/D407/02/06        | Second Lane of Gawaragiriya Kolambewa Road                  | 158383.129/143228.229                          | 158383.713/143232.571 | 158576.865/143284.811                     | 158574.171/143288.034 | 237.37                     | 4.2                       | 2.8                                 |
| 289        | SG/APS/B034/<br>C404/D407/02/07        | Third Lane of Gawaragiriya Kolambewa Road                   | 158282.665/143540.767                          | 158278.032/143541.949 | 158197.617/144086.884                     | 158196.338/144089.597 | 652.69                     | 3.0                       | 3.0                                 |

| Serial No. | Code of the Road                       | Name of the Road                                                    | Starting Coordinates<br>(Kandawala Sri Lanka ) |                       | Ending Coordinates<br>(Kandawala Sri Lanka ) |                       | Length of the Road (Meter) | Width of the Road (Meter) | Developed Width of the Road (Meter) |
|------------|----------------------------------------|---------------------------------------------------------------------|------------------------------------------------|-----------------------|----------------------------------------------|-----------------------|----------------------------|---------------------------|-------------------------------------|
|            |                                        |                                                                     | Left                                           | Right                 | Left                                         | Right                 |                            |                           |                                     |
| 290        | SG/APS/B034/<br>C404/D407/03           | First Lane of<br>Gawaragiriya<br>Munihinkanda Road                  | 160070.308/144121.318                          | 160074.095/144115.104 | 159968.153/144113.02                         | 159970.943/144111.919 | 150.67                     | 3.0                       | 2.5                                 |
| 291        | SG/APS/B034/<br>C404/D407/04           | Second Lane of<br>Gawaragiriya<br>Munihinkanda Road                 | 159794.826/144264.634                          | 159797.389/144263.063 | 159768.364/144244.475                        | 159770.02/144241.973  | 36.26                      | 3.0                       | 2.5                                 |
| 292        | SG/APS/B034/<br>C404/D407/05           | Third Lane of<br>Gawaragiriya<br>Munihinkanda Road                  | 159666.649/144453.8                            | 159663.63/144455.816  | 159807.424/144467.393                        | 159805.364/144469.573 | 164.01                     | 3.0                       | 2.5                                 |
| 293        | SG/APS/B034/<br>C404/D407/06           | Fourth Lane of<br>Gawaragiriya<br>Munihinkanda Road                 | 159448.12/144509.898                           | 159444.09/144510.486  | 159608.707/144592.149                        | 159610.995/144595.43  | 316.5                      | 4.0                       | 3.0                                 |
| 294        | SG/APS/B034/<br>C404/D407/06/01        | First Subway of Fourth<br>Lane of Gawaragiriya<br>Munihinkanda Road | 159546.329/144610.2                            | 159541.403/144611.997 | 159544.549/144642.438                        | 159540.597/144643.056 | 35.18                      | 4.0                       | 3.0                                 |
| 295        | SG/APS/B034/<br>C404/D407/07           | Kolambewa<br>Munihinkanda<br>Ihalakanda Road                        | 158971.526/144597.328                          | 158969.03/144594.416  | 158120.112/145533.83                         | 158116.754/145532.053 | 1357.05                    | 3.8                       | 3.0                                 |
| 296        | SG/APS/B034/<br>C404/D407/07/01        | First Lane of<br>Kolambewa<br>Munihinkanda<br>Ihalakanda Road       | 158847.003/144733.997                          | 158845.258/144738.239 | 159039.194/144981.19                         | 159036.634/144983.272 | 428.42                     | 3.3                       | 3.0                                 |
| 297        | SG/APS/B034/<br>C404/D407/07/02        | Kolambewa<br>Munihinkanda<br>Dodangewaththa Road                    | 158696.391/144884.86                           | 158699.492/144883.193 | 158634.513/144675.817                        | 158636.259/144678.85  | 242.44                     | 3.5                       | 2.8                                 |
| 298        | SG/APS/B034/<br>C404/D407/07/03        | Fifth Lane of<br>Kolambewa<br>Munihinkanda                          | 158542.604/145028.014                          | 158538.637/145030.686 | 158714.365/145131.924                        | 158714.169/145134.917 | 392.11                     | 3.0                       | 2.5                                 |
| 299        | SG/APS/<br>B034/C404/<br>D407/07/03/01 | First By Pass of<br>Munihinkanda Fifth<br>Lane                      | 158590.991/145201.086                          | 158587.689/145201.461 | 158695.52/145353.7                           | 158696.379/145356.574 | 601.07                     | 3.0                       | 2.5                                 |
| 300        | SG/APS/B034/<br>C404/D407/08           | Sixth Lane of<br>Kolambewa<br>Munihinkanda                          | 158866.522/144388.389                          | 158865.883/144385.255 | 158610.211/144338.245                        | 158608.168/144336.049 | 291.71                     | 3.0                       | 2.5                                 |
| 301        | SG/APS/B034/<br>C404/C401/01           | Landemedahena Road                                                  | 163569.417/141308.403                          | 163565.619/141309.094 | 163332.674/141668.101                        | 163331.132/141664.958 | 469.6                      | 3.5                       | 2.5                                 |

| Serial No. | Code of the Road                  | Name of the Road                                      | Starting Coordinates<br>(Kandawala Sri Lanka ) |                       | Ending Coordinates (Kandawala Sri Lanka ) |                       | Length of the Road (Meter) | Width of the Road (Meter) | Developed Width of the Road (Meter) |
|------------|-----------------------------------|-------------------------------------------------------|------------------------------------------------|-----------------------|-------------------------------------------|-----------------------|----------------------------|---------------------------|-------------------------------------|
|            |                                   |                                                       | Left                                           | Right                 | Left                                      | Right                 |                            |                           |                                     |
| 302        | SG/APS/B034/C404/C401/02          | Dumbara Manana Kaluwahena Road                        | 163944.518/141303.777                          | 163948.493/141304.248 | 166245.219/139702.94                      | 166244.348/139706.936 | 3549.34                    | 4.0                       | 3.5                                 |
| 303        | SG/APS/B034/C404/C401/02/01       | First Lane of Mahawalawaththa Pahala                  | 166002.781/139632.525                          | 166010.627/139627.027 | 164611.691/139486.328                     | 164611.307/139482.347 | 1750.26                    | 4.0                       | 2.5                                 |
| 304        | SG/APS/B034/C404/C401/02/01/01    | First Lane of Mahawalawaththa West                    | 165888.461/139579.195                          | 165892.671/139580.48  | 165866.895/139267.512                     | 165870.825/139266.768 | 458.09                     | 4.0                       | 3.0                                 |
| 305        | SG/APS/B034/C404/C401/02/01/02    | Second Lane of Mahawalawaththa Pahala                 | 165627.987/139570.743                          | 165623.85/139571.777  | 165642.93/139611.545                      | 165640.391/139614.636 | 48.85                      | 4.0                       | 3.0                                 |
| 306        | SG/APS/B034/C404/C401/02/01/03    | Second Lane of Mahawalawaththa West                   | 165489.395/139597.805                          | 165494.258/139595.241 | 165390.308/139350.989                     | 165393.146/139353.809 | 406.11                     | 4.0                       | 2.5                                 |
| 307        | SG/APS/B034/C404/C401/02/01/04    | Third Lane of Mahawalawaththa Pahala                  | 165321.014/139668.669                          | 165316.721/139668.115 | 165302.971/139736.613                     | 165299.871/139734.989 | 72.95                      | 3.5                       | 2.5                                 |
| 308        | SG/APS/B034/C404/C401/02/01/05    | Sodurukanda Road                                      | 164924.12/139470.482                           | 164918.59/139471.973  | 164709.911/139695.183                     | 164708.337/139691.506 | 434.5                      | 4.0                       | 2.5                                 |
| 309        | SG/APS/B034/C404/C401/02/02       | Dumbara Road No. 02                                   | 166065.85/139574.914                           | 166069.315/139571.639 | 167182.273/138722.521                     | 167178.712/138720.7   | 2153.66                    | 4.0                       | 2.5                                 |
| 310        | SG/APS/B034/C404/C401/02/02/01    | First Lane of Dumbara Road No. 02                     | 166130.695/139486.064                          | 166134.467/139484.669 | 166278.353/139166.614                     | 166282.224/139165.607 | 384.13                     | 4.0                       | 2.5                                 |
| 311        | SG/APS/B034/C404/C401/02/02/01/01 | First By Pass of the First Lane of Dumbara Road No.02 | 166146.247/139397.065                          | 166152.835/139391.805 | 166076.601/139392.33                      | 166075.03/139389.773  | 127.38                     | 3.0                       | 2.5                                 |
| 312        | SG/APS/B034/C404/C401/03          | Dumbara Manana Kuttikanda Road                        | 164164.67/141345.967                           | 164158.941/141346.65  | 165891.23/142114.353                      | 165896.228/142114.522 | 5413.49                    | 5.0                       | 2.5                                 |
| 313        | SG/APS/B034/C404/C401/03/01       | No. 01 Dumbara Manana Road                            | 164536.479/141436.909                          | 164537.5/141440.87    | 167409.194/139926.99                      | 167413.289/139928.864 | 3909.45                    | 4.0                       | 2.5                                 |
| 314        | SG/APS/B034/C404/C401/03/02       | Dumbara Manana Pathalmandiya Road                     | 164380.898/141542.213                          | 164377.625/141544.513 | 164052.052/142374.41                      | 164051.034/142370.542 | 1216.5                     | 4.0                       | 2.6                                 |
| 315        | SG/APS/B034/C404/C401/03/02/01    | First Lane of Dumbara Manana Pathalmandiya Road       | 164459.644/141680.811                          | 164456.362/141678.194 | 164138.131/141911.672                     | 164137.558/141907.714 | 427.07                     | 4.0                       | 3.0                                 |

| Serial No. | Code of the Road                          | Name of the Road                                       | Starting Coordinates<br>(Kandawala Sri Lanka ) |                       | Ending Coordinates<br>(Kandawala Sri Lanka ) |                       | Length of the Road<br>(Meter) | Width of the Road<br>(Meter) | Developed Width<br>of the Road (Meter) |
|------------|-------------------------------------------|--------------------------------------------------------|------------------------------------------------|-----------------------|----------------------------------------------|-----------------------|-------------------------------|------------------------------|----------------------------------------|
|            |                                           |                                                        | Left                                           | Right                 | Left                                         | Right                 |                               |                              |                                        |
| 316        | SG/APS/<br>B034/C404/<br>C401/03/02/02    | Second Lane of<br>Dumbara Manana<br>Pathalmandiya Road | 164531.977/141828.718                          | 164529.88/141831.622  | 164643.566/142030.531                        | 164640.092/142030.108 | 257.64                        | 3.5                          | 2.5                                    |
| 317        | SG/APS/<br>B034/C404/<br>C401/03/02/02/01 | Dumbara Manana<br>Miyangala Kurunda<br>Road            | 164636.291/141954.722                          | 164634.939/141959.151 | 165198.71/141807.634                         | 165202.07/141804.641  | 631.81                        | 4.5                          | 2.5                                    |
| 318        | SG/APS/<br>B034/C404/<br>C401/03/02/03    | Third Lane of Dumbara<br>Manana Pathalmandiya<br>Road  | 164258.957/142003.341                          | 164262.152/141997.765 | 164100.798/142116.06                         | 164099.281/142112.905 | 209.33                        | 3.5                          | 2.5                                    |
| 319        | SG/APS/B034/<br>C404/C401/03/03           | First Lane of Dumbara<br>Manana Kuttikanda<br>Road     | 163635.671/142357.046                          | 163633.06/142355.555  | 163354.38/142662.842                         | 163352.065/142660.933 | 437.79                        | 3.0                          | 2.5                                    |
| 320        | SG/APS/B034/<br>C404/C401/03/04           | Dumbara Manana<br>Akkara 08 Road                       | 163841.381/142762.389                          | 163843.517/142765.997 | 164050.29/142644.156                         | 164052.236/142640.66  | 284.95                        | 4.0                          | 2.6                                    |
| 321        | SG/APS/B034/<br>C404/C401/03/05           | Second Lane of<br>Dumbara Manana<br>Kuttikanda Road    | 164428.871/142945.801                          | 164432.902/142942.32  | 164393.2/142868.601                          | 164393.885/142864.66  | 122.87                        | 4.0                          | 3.0                                    |
| 322        | SG/APS/B034/<br>C404/C401/04              | No.82 , Road near Kovil                                | 166942.524/139483.98                           | 166935.276/139486.901 | 167628.782/139477.376                        | 167628.157/139480.819 | 733.48                        | 3.5                          | 2.5                                    |
| 323        | SG/APS/B034/<br>C404/C401/05              | Footpath No.82<br>Dumbara                              | 167105.569/139423.374                          | 167107.583/139422.322 | 167227.378/138954.551                        | 167229.145/138955.489 | 777.67                        | 2.0                          | 1.5                                    |
| 324        | SG/APS/B034/<br>C404/C401/06              | Dumbara No. 01 Road                                    | 168182.573/138870.069                          | 168182.06/138874.932  | 167809.426/140441.934                        | 167805.474/140442.553 | 2313.73                       | 4.0                          | 3.0                                    |
| 325        | SG/APS/B034/<br>C404/C401/07              | Dumbara Medikella<br>Ihala Road                        | 168219.125/138592.16                           | 168214.867/138602.546 | 168972.466/138633.193                        | 168973.006/138637.156 | 1081.8                        | 4.0                          | 2.5                                    |
| 326        | SG/APS/B034/<br>C404/C401/08              | Minipura Dumbara<br>Road                               | 168635.217/138228.821                          | 168631.853/138226.142 | 168544.386/138262.959                        | 168540.747/138261.297 | 115.54                        | 4.0                          | 3.0                                    |
| 327        | SG/APS/B034/<br>C404/C401/09              | Minipura Dumbara<br>Ethaereliyagoda Road               | 168751.409/138073.939                          | 168755.543/138073.175 | 168033.794/138501.759                        | 168029.868/138502.53  | 1095.3                        | 4.0                          | 2.6                                    |
| 328        | SG/APS/B034/<br>C404/C401/10              | Penigalawaththa<br>Thotupala Road                      | 168799.218/137902.52                           | 168802.731/137898.96  | 170067.609/137559.462                        | 170064.276/137563.216 | 4084.85                       | 5.0                          | 2.6                                    |
| 329        | SG/APS/B034/<br>C404/C401/10/01           | Dumbara Kaluwala<br>Road                               | 168157.401/137774.094                          | 168157.087/137769.89  | 167997.597/138114.812                        | 167995.529/138117.635 | 472.76                        | 3.5                          | 2.5                                    |
| 330        | SG/APS/B034/<br>C404/C401/10/02           | First Lane of<br>Penigalawaththa<br>Thotupala Road     | 168309.105/137506.554                          | 168316.913/137504.135 | 168229.945/137508.79                         | 168226.846/137506.262 | 98.39                         | 4.0                          | 3.0                                    |

| Serial No. | Code of the Road                | Name of the Road                                    | Starting Coordinates<br>(Kandawala Sri Lanka ) |                       | Ending Coordinates (Kandawala Sri Lanka ) |                       | Length of the Road (Meter) | Width of the Road (Meter) | Developed Width of the Road (Meter) |
|------------|---------------------------------|-----------------------------------------------------|------------------------------------------------|-----------------------|-------------------------------------------|-----------------------|----------------------------|---------------------------|-------------------------------------|
|            |                                 |                                                     | Left                                           | Right                 | Left                                      | Right                 |                            |                           |                                     |
| 331        | SG/APS/B034/<br>C404/C401/10/03 | Penigalawaththa<br>Halwathura Road                  | 168712.289/137288.585                          | 168716.23/137284.514  | 168665.296/137188.45                      | 168669.989/137186.726 | 115.29                     | 5.0                       | 2.6                                 |
| 332        | SG/APS/B034/<br>C404/C401/10/04 | Second Lane of<br>Penigalawaththa<br>Thotupala Road | 168947.665/137212.914                          | 168953.147/137210.257 | 168966.707/137126.2                       | 168969.474/137128.342 | 101.26                     | 3.5                       | 2.0                                 |
| 333        | SG/APS/B034/<br>C404/C401/10/05 | Third Lane of<br>Penigalawaththa<br>Thotupala Road  | 169420.173/137141.16                           | 169423.788/137141.825 | 169384.294/136898.167                     | 169387.592/136899.342 | 257.57                     | 3.5                       | 2.5                                 |
| 334        | SG/APS/B034/<br>C404/C401/10/06 | Fourth Lane of<br>Penigalawaththa<br>Thotupala Road | 169946.902/137056.331                          | 169951.315/137055.014 | 169858.152/136653.153                     | 169858.993/136649.243 | 651.13                     | 4.0                       | 2.1                                 |
| 335        | SG/APS/B034/<br>C404/C401/10/07 | Fifth Lane of<br>Penigalawaththa<br>Thotupala Road  | 169954.559/137054.354                          | 169959.449/137054.23  | 170064.331/136947.26                      | 170068.922/136946.957 | 176.83                     | 4.6                       | 4.0                                 |
| 336        | SG/APS/B034/<br>C404/C401/11    | Domsiyawaththa<br>Thotupala Road                    | 169590.917/138087.129                          | 169585.055/138097.712 | 170081.326/137540.973                     | 170084.233/137543.72  | 988.19                     | 4.0                       | 2.5                                 |
| 337        | SG/APS/B034/<br>C404/C401/12    | Medapala Road No.01                                 | 169568.796/138653.691                          | 169568.472/138644.097 | 167450.006/139959.141                     | 167446.501/139953.649 | 2699.67                    | 3.5                       | 2.5                                 |
| 338        | SG/APS/B034/<br>C404/C401/13    | Pahalapola First Road                               | 169603.301/138783.925                          | 169616.912/138787.77  | 169853.565/138550.38                      | 169855.909/138554.916 | 366.21                     | 5.0                       | 2.5                                 |
| 339        | SG/APS/B034/<br>C404/C401/14    | Pahalapola Second Road                              | 169959.605/138553.252                          | 169964.691/138549.087 | 170148.286/138438.809                     | 170149.175/138442.708 | 455.02                     | 4.0                       | 3.0                                 |
| 340        | SG/APS/B034/<br>C404/C401/14/01 | First Lane of Pahalapola<br>Second Road             | 169880.599/138506.303                          | 169884.09/138506.695  | 170065.251/138101.546                     | 170068.631/138102.455 | 515.72                     | 3.5                       | 2.5                                 |
| 341        | SG/APS/B034/<br>C404/C401/14/02 | Second Lane of<br>Pahalapola Second Road            | 170042.718/138459.316                          | 170045.674/138458.35  | 170006.107/138388.362                     | 170008.808/138386.793 | 87.99                      | 3.0                       | 2.0                                 |
| 342        | SG/APS/B034/<br>C404/C401/14/03 | Third Lane of<br>Pahalapola Second Road             | 170120.979/138439.662                          | 170123.481/138439.708 | 170025.403/138374.488                     | 170027.377/138372.639 | 135.11                     | 2.5                       | 2.5                                 |
| 343        | SG/APS/B034/<br>C404/C401/15    | Pahalapola Third Road                               | 170094.887/138614.153                          | 170098.645/138615.552 | 170189.197/138604.204                     | 170185.914/138606.488 | 120.09                     | 4.0                       | 2.5                                 |
| 344        | SG/APS/B034/<br>C404/C401/15/01 | First Lane of Pahalapola<br>Third Road              | 170108.994/138589.081                          | 170111.809/138586.657 | 170121.508/138443.672                     | 170124.792/138443.741 | 163.95                     | 3.0                       | 2.5                                 |
| 345        | SG/APS/B034/<br>C402/01         | First Lane of Ayagama<br>Elapatha Road              | 159461.777/149379.181                          | 159458.973/149381.326 | 159387.298/149574.851                     | 159385.347/149571.943 | 256.14                     | 3.5                       | 3.0                                 |


| Serial No. | Code of the Road              | Name of the Road                                           | Starting Coordinates<br>(Kandawala Sri Lanka ) |                       | Ending Coordinates<br>(Kandawala Sri Lanka ) |                       | Length of the<br>Road (Meter) | Width of the Road<br>(Meter) | Developed Width<br>of the Road (Meter) |
|------------|-------------------------------|------------------------------------------------------------|------------------------------------------------|-----------------------|----------------------------------------------|-----------------------|-------------------------------|------------------------------|----------------------------------------|
|            |                               |                                                            | Left                                           | Right                 | Left                                         | Right                 |                               |                              |                                        |
| 346        | SG/APS/B034/<br>C402/01/01    | First By Pass of First<br>Lane of Ayagama<br>Elapatha Road | 159423.585/149522.478                          | 159424.399/149525.883 | 159502.077/149478.071                        | 159503.732/149481.156 | 93.1                          | 3.5                          | 3.0                                    |
| 347        | SG/APS/B034/<br>C402/02       | Sarathpuraya Central<br>Road                               | 159447.649/149388.194                          | 159450.001/149384.943 | 159232.965/149320.121                        | 159236.74/149318.507  | 300.32                        | 4.0                          | 3.0                                    |
| 348        | SG/APS/B034/<br>C402/02/01    | First Lane of<br>Sarathpuraya Central<br>Road              | 159382.923/149306.953                          | 159382.727/149304.453 | 159306.148/149352.255                        | 159304.278/149350.595 | 93.78                         | 2.5                          | 1.0                                    |
| 349        | SG/APS/B034/<br>C402/02/02    | Second Lane of<br>Sarathpuraya Central<br>Road             | 159255.574/149335.976                          | 159252.454/149334.811 | 159277.353/149390.737                        | 159276.866/149393.697 | 66.48                         | 3.0                          | 3.0                                    |
| 350        | SG/APS/B034/<br>C402/03       | First Lane of<br>Sarathpuraya                              | 159381.676/149465.264                          | 159383.42/149462.67   | 159240.917/149429.631                        | 159241.003/149426.547 | 155.78                        | 3.0                          | 3.0                                    |
| 351        | SG/APS/B034/<br>C402/04       | Second Lane of<br>Ayagama Elapatha Road                    | 159389.948/149582.055                          | 159387.143/149580.654 | 159326.662/149723.997                        | 159323.688/149723.605 | 197.56                        | 3.0                          | 3.0                                    |
| 352        | SG/APS/B034/<br>C402/05       | Third Road of Ayagama<br>Elapatha Road                     | 159537.463/149681.071                          | 159537.114/149684.57  | 159592.073/149643.185                        | 159591.783/149646.672 | 75.32                         | 3.5                          | 3.5                                    |
| 353        | SG/APS/B034/<br>C402/06       | Fourth Road of<br>Ayagama Elapatha Road                    | 159510.747/149768.346                          | 159511.485/149764.748 | 159257.203/149882.453                        | 159256.039/149879.153 | 316.02                        | 3.5                          | 3.5                                    |
| 354        | SG/APS/B034/<br>C402/07       | Samarugama Central<br>Road                                 | 159379.418/149957.766                          | 159379.92/149954.302  | 159165.735/149699.736                        | 159169.01/149701.016  | 493.07                        | 3.5                          | 3.0                                    |
| 355        | SG/APS/B034/<br>C402/08       | Fifth Road of Ayagama<br>Elapatha Road                     | 159279.654/150104.126                          | 159277.422/150106.134 | 159689.449/149943.843                        | 159686.7/149945.045   | 505.46                        | 3.0                          | 3.0                                    |
| 356        | SG/APS/B034/<br>C402/09       | Sixth Road of Ayagama<br>Elapatha Road                     | 159128.731/150373.43                           | 159126.751/150370.511 | 158792.732/150542.001                        | 158795.844/150540.399 | 578.75                        | 3.5                          | 3.0                                    |
| 357        | SG/APS/B034/<br>C402/10       | Seventh Road of<br>Ayagama Elapatha Road                   | 159741.171/150667.187                          | 159740.058/150670.378 | 160130.92/150920.892                         | 160129.531/150923.551 | 613.49                        | 3.0                          | 3.0                                    |
| 358        | SG/APS/B034/<br>D401/01       | Udugala Gendagala<br>Road                                  | 157287.745/150320.142                          | 157291.64/150321.053  | 156313.654/146716.075                        | 156316.312/146713.085 | 5197.59                       | 4.0                          | 3.5                                    |
| 359        | SG/APS/B034/<br>D401/01/01    | Finehill Estate Road                                       | 157208.055/150206.886                          | 157209.151/150203.024 | 156709.13/150088.967                         | 156713.044/150089.79  | 1057.62                       | 4.0                          | 4.0                                    |
| 360        | SG/APS/B034/<br>D401/01/02    | Finehill Colony Road                                       | 157320.013/149886.172                          | 157317.269/149883.871 | 156982.264/149661.686                        | 156985.239/149659.842 | 566.71                        | 3.5                          | 3.0                                    |
| 361        | SG/APS/B034/<br>D401/01/02/01 | Finehill Ihala Road                                        | 157227.648/149894.143                          | 157225.013/149892.709 | 157160.356/149888.568                        | 157163.081/149887.312 | 95.31                         | 3.0                          | 3.0                                    |


| Serial No. | Code of the Road              | Name of the Road                                | Starting Coordinates<br>(Kandawala Sri Lanka ) |                       | Ending Coordinates (Kandawala Sri Lanka ) |                       | Length of the Road (Meter) | Width of the Road (Meter) | Developed Width of the Road (Meter) |
|------------|-------------------------------|-------------------------------------------------|------------------------------------------------|-----------------------|-------------------------------------------|-----------------------|----------------------------|---------------------------|-------------------------------------|
|            |                               |                                                 | Left                                           | Right                 | Left                                      | Right                 |                            |                           |                                     |
| 362        | SG/APS/B034/<br>D401/01/02/02 | Finehill Colony<br>Gendagala Road               | 157133.609/149725.826                          | 157137.132/149726.868 | 157065.731/149589.514                     | 157069.925/149590.522 | 159.34                     | 3.0                       | 2.0                                 |
| 363        | SG/APS/B034/<br>D401/01/02/03 | First Lane of Finehill<br>Colony Gendagala Road | 157030.221/149714.53                           | 157027.327/149713.727 | 156910.603/149791.995                     | 156908.828/149789.577 | 189.46                     | 3.0                       | 3.0                                 |
| 364        | SG/APS/B034/<br>D401/01/03    | Udugala Pitakanda<br>Gamsabha First Road        | 157326.54/149849.629                           | 157323.621/149852.496 | 157404.109/149821.606                     | 157407.586/149823.594 | 114.46                     | 4.0                       | 3.0                                 |
| 365        | SG/APS/B034/<br>D401/01/04    | Udugala Pitakanda<br>Gamsabha Second Road       | 157324.255/149782.296                          | 157324.224/149785.299 | 157456.781/149792.983                     | 157456.728/149795.982 | 155.48                     | 3.0                       | 3.0                                 |
| 366        | SG/APS/B034/<br>D401/01/05    | Bubulahena Road                                 | 157310.794/149645.707                          | 157312.533/149648.173 | 157543.494/149446.695                     | 157542.715/149449.591 | 352.37                     | 3.0                       | 2.0                                 |
| 367        | SG/APS/B034/<br>D401/01/06    | Udugala Gendagala<br>Gamsabha Road              | 157154.466/149534.557                          | 157151.607/149533.449 | 156816.662/149478.874                     | 156818.62/149481.149  | 472.18                     | 3.0                       | 2.0                                 |
| 368        | SG/APS/B034/<br>D401/01/07    | Kaluthara Elawellahena<br>Road                  | 156822.356/149378.184                          | 156821.703/149375.114 | 156698.037/149406.824                     | 156696.315/149404.368 | 132.69                     | 3.0                       | 3.0                                 |
| 369        | SG/APS/B034/<br>D401/01/08    | First Lane of Udugala<br>Gendagala Road         | 156811.451/149337.844                          | 156811.69/149334.842  | 156763.994/149303.041                     | 156765.413/149300.397 | 63.81                      | 3.0                       | 3.0                                 |
| 370        | SG/APS/B034/<br>D401/01/09    | Gendagala Old<br>Gamsabha Road                  | 156684.691/148304.064                          | 156681.118/148302.226 | 156549.574/148301.897                     | 156552.931/148304.161 | 182.36                     | 4.0                       | 4.0                                 |
| 371        | SG/APS/B034/<br>D401/01/10    | Gendagala Aranya Road                           | 156663.245/147217.589                          | 156663.011/147221.128 | 156856.926/147066.015                     | 156858.919/147068.892 | 256.08                     | 3.5                       | 3.0                                 |
| 372        | SG/APS/B034/<br>D401/01/11    | Gendagala Hathaliha<br>Waththa Road             | 156531.734/147168.814                          | 156534.705/147170.276 | 156588.076/146855.55                      | 156590.973/146856.33  | 350.74                     | 3.0                       | 2.5                                 |
| 373        | SG/APS/B034/<br>D401/01/12    | Gendagala Millahena<br>Footpath                 | 156514.649/147164.072                          | 156512.859/147162.653 | 156399.529/147315.415                     | 156397.529/147315.453 | 267.89                     | 2.0                       | 1.0                                 |
| 374        | SG/APS/B034/<br>D401/01/13    | Gendagala Millahena<br>Road                     | 156465.693/147104.555                          | 156464.318/147100.354 | 155868.854/147300.375                     | 155871.845/147303.031 | 1164.3                     | 4.0                       | 3.0                                 |
| 375        | SG/APS/B034/<br>D401/01/13/01 | First Lane of Gendagala<br>Millahena Road       | 155798.488/147446.75                           | 155800.358/147442.241 | 155757.427/147412.9                       | 155760.911/147413.242 | 106.04                     | 3.5                       | 2.5                                 |
| 376        | SG/APS/B034/<br>D401/01/14    | Hulkiridola Power<br>House Road                 | 156317.778/146714.349                          | 156320.348/146716.86  | 157384.536/146089.61                      | 157388.032/146089.765 | 1505.66                    | 3.5                       | 2.5                                 |
| 377        | SG/APS/B034/<br>D401/02       | First Lane of Udugala<br>Anguruwela Road        | 157148.367/150420.874                          | 157150.959/150419.323 | 156956.706/150276.248                     | 156955.504/150273.499 | 276.08                     | 3.0                       | 3.0                                 |
| 378        | SG/APS/B034/<br>D401/02/01    | Sri<br>Dharmarakshitharamaya<br>Road            | 157080.52/150372.702                           | 157078.667/150369.666 | 157022.099/150382.247                     | 157020.6/150379.648   | 61.74                      | 3.0                       | 3.0                                 |





| Serial No. | Code of the Road           | Name of the Road                                      | Starting Coordinates<br>(Kandawala Sri Lanka ) |                       | Ending Coordinates<br>(Kandawala Sri Lanka ) |                       | Length of the<br>Road (Meter) | Width of the Road<br>(Meter) | Developed Width<br>of the Road (Meter) |
|------------|----------------------------|-------------------------------------------------------|------------------------------------------------|-----------------------|----------------------------------------------|-----------------------|-------------------------------|------------------------------|----------------------------------------|
|            |                            |                                                       | Left                                           | Right                 | Left                                         | Right                 |                               |                              |                                        |
| 379        | SG/APS/B034/<br>D401/03    | Second Lane of Udugala<br>Anguruwela Road             | 156827.768/150588.171                          | 156824.818/150587.482 | 156791.117/150679.513                        | 156788.524/150678.006 | 102.04                        | 3.0                          | 3.0                                    |
| 380        | SG/APS/B034/<br>D401/04    | First Road of<br>Anguruwela Finehill<br>Waththa       | 156693.755/150550.761                          | 156696.529/150551.993 | 156751.097/150216.214                        | 156753.191/150218.367 | 546.79                        | 3.0                          | 2.5                                    |
| 381        | SG/APS/B034/<br>D401/05    | Third Lane of Udugala<br>Anguruwela Road              | 156584.485/150624.643                          | 156582.288/150627.259 | 156643.239/150734.101                        | 156640.736/150732.446 | 153.86                        | 3.0                          | 2.5                                    |
| 382        | SG/APS/B034/<br>D401/06    | Handunkanda<br>Batahena Road                          | 156040.438/150792.897                          | 156036.998/150795.111 | 156122.938/150988.518                        | 156122.743/150992.513 | 327.12                        | 4.0                          | 2.6                                    |
| 383        | SG/APS/B034/<br>D401/06/01 | First Lane of<br>Handunkanda Batahena<br>Road         | 156062.901/151020.222                          | 156058.403/151020.36  | 156121.892/151137.242                        | 156119.409/151140.995 | 157.53                        | 4.5                          | 2.0                                    |
| 384        | SG/APS/B034/<br>D401/07    | Handunkanda School<br>Road                            | 155993.968/150808.67                           | 155990.983/150808.333 | 155932.163/150913.026                        | 155929.876/150914.969 | 152.82                        | 3.0                          | 2.0                                    |
| 385        | SG/APS/B034/<br>D401/08    | First Lane of<br>Handunkanda                          | 155941.04/150567.698                           | 155942.719/150571.068 | 156052.536/150397.226                        | 156055.058/150399.652 | 219.62                        | 3.5                          | 2.5                                    |
| 386        | SG/APS/B034/<br>D401/09    | Second Road of<br>Anguruwela Finehill<br>Waththa Road | 155416.689/150299.172                          | 155423.355/150297.887 | 156700.848/150198.96                         | 156696.86/150194.851  | 2147.1                        | 4.0                          | 2.5                                    |
| 387        | SG/APS/B034/<br>D401/10    | Fourth Lane of Udugala<br>Anguruwela Road             | 155255.126/150278.066                          | 155258.442/150279.193 | 155301.796/150099.024                        | 155303.867/150101.844 | 238.52                        | 3.5                          | 3.0                                    |
| 388        | SG/APS/B034/<br>D401/11    | Anguruwela Tank<br>Footpath                           | 154924.975/150380.579                          | 154922.681/150383.016 | 154917.22/151066.195                         | 154917.112/151069.193 | 975.28                        | 3.0                          | 2.0                                    |
| 389        | SG/APS/B034/<br>D401/12    | First Lane of<br>Panwilahena                          | 154663.695/150905.562                          | 154663.531/150901.319 | 154547.724/151089.588                        | 154544.204/151091.487 | 247.05                        | 4.0                          | 3.0                                    |
| 390        | SG/APS/B034/<br>D401/13    | Anguruwela<br>Panwilahena Road                        | 154671.092/150934.792                          | 154668.105/150935.088 | 154379.255/151278.751                        | 154379.522/151275.763 | 586.84                        | 3.0                          | 3.0                                    |
| 391        | SG/APS/B034/<br>D401/13/01 | Panwilahena Second<br>Lane - Footpath                 | 154643.94/151182.473                           | 154640.685/151184.567 | 154534.83/151309.855                         | 154534.658/151306.859 | 211.24                        | 3.0                          | 1.0                                    |
| 392        | SG/APS/B034/<br>C403/01    | Weragamkanda Road                                     | 153527.299/154057.44                           | 153527.251/154061.441 | 154282.721/153664.727                        | 154279.844/153667.505 | 989.79                        | 4.0                          | 4.0                                    |


| Serial No. | Code of the Road           | Name of the Road                                 | Starting Coordinates<br>(Kandawala Sri Lanka ) |                       | Ending Coordinates<br>(Kandawala Sri Lanka ) |                       | Length of the Road (Meter) | Width of the Road (Meter) | Developed Width of the Road (Meter) |
|------------|----------------------------|--------------------------------------------------|------------------------------------------------|-----------------------|----------------------------------------------|-----------------------|----------------------------|---------------------------|-------------------------------------|
|            |                            |                                                  | Left                                           | Right                 | Left                                         | Right                 |                            |                           |                                     |
| 393        | SG/APS/B034/<br>C403/02    | Kukuluwa Rajamaha<br>Vihara First Mawatha        | 153415.092/154520.334                          | 153416.359/154526.083 | 154548.876/155593.224                        | 154549.724/155596.62  | 2129.06                    | 3.5                       | 3.0                                 |
| 394        | SG/APS/B034/<br>C403/02/01 | Karawilohenyaya Road                             | 153688.552/154709.874                          | 153688.286/154714.284 | 153796.476/154135.909                        | 153799.374/154136.687 | 788.25                     | 3.0                       | 2.5                                 |
| 395        | SG/APS/B034/<br>C403/03    | Wellawaththa Nawinna<br>Road                     | 153491.897/154877.567                          | 153490.694/154874.125 | 153259.975/154932.132                        | 153257.195/154930.006 | 306.89                     | 3.5                       | 3.0                                 |
| 396        | SG/APS/B034/<br>C403/04    | Kukuluwa Rajamaha<br>Vihara Footpath             | 153515.858/154959.691                          | 153515.612/154961.225 | 153738.211/155002.228                        | 153738.768/155003.684 | 247.55                     | 1.5                       | 1.5                                 |
| 397        | SG/APS/B034/<br>C403/05    | Nawinnawaththa<br>Dewala Road                    | 153482.602/155076.016                          | 153484.102/155072.29  | 153258.283/155086.651                        | 153261.462/155085.185 | 312.38                     | 3.5                       | 3.5                                 |
| 398        | SG/APS/B034/<br>C403/06    | Nawinnawaththa<br>Kurahana Road                  | 153329.396/155519.527                          | 153332.445/155516.448 | 153150.443/155626.267                        | 153150.56/155630.266  | 364.51                     | 4.0                       | 3.0                                 |
| 399        | SG/APS/B034/<br>C403/06/01 | Nawinnawaththa<br>Madiththa Road                 | 153156.402/155509.905                          | 153159.597/155508.082 | 152728.705/15535356.83                       | 152726.554/155354.461 | 1343.14                    | 3.2                       | 3.0                                 |
| 400        | SG/APS/B034/<br>C403/07    | Pimbura Katwana Road                             | 153417.591/155745.569                          | 153416.569/155740.593 | 152709.9/156242.322                          | 152708.631/156237.485 | 1060.64                    | 5.0                       | 4.0                                 |
| 401        | SG/APS/B034/<br>C403/07/01 | Thennahena Road                                  | 152870.605/156202.46                           | 152865.714/156201.659 | 153234.208/156678.36                         | 153231.423/156675.489 | 1137.57                    | 4.0                       | 3.0                                 |
| 402        | SG/APS/B034/<br>C403/08    | Kukuluwa Rajamaha<br>Vihara Second Road          | 153463.565/156000.401                          | 153462.728/156003.372 | 154024.251/155442.209                        | 154026.865/155440.112 | 864.91                     | 3.0                       | 3.0                                 |
| 403        | SG/APS/B034/<br>C403/09    | First Lane of Pimbura<br>Karawita Road           | 153460.226/156158.501                          | 153460.447/156165.711 | 153510.578/156229.595                        | 153508.374/156232.314 | 90.02                      | 3.5                       | 3.0                                 |
| 404        | SG/APS/B034/<br>C403/10    | Second Lane of Pimbura<br>Karawita Road          | 153459.349/156263.282                          | 153460.227/156267.562 | 153532.008/156308.444                        | 153530.977/156311.79  | 89.52                      | 3.5                       | 3.0                                 |
| 405        | SG/APS/B421/<br>C428/01    | First Road of<br>Kukulegama<br>Jathuwangoda Road | 153463.408/150016.386                          | 153462.085/150021.274 | 154167.955/149520.647                        | 154171.478/149517.099 | 979.21                     | 5.0                       | 3.0                                 |
| 406        | SG/APS/B421/<br>C428/02    | Nidangala Temple Road                            | 153121.918/149082.771                          | 153121.754/149078.768 | 152640.684/149889.154                        | 152636.832/149890.232 | 1216.06                    | 4.0                       | 2.5                                 |

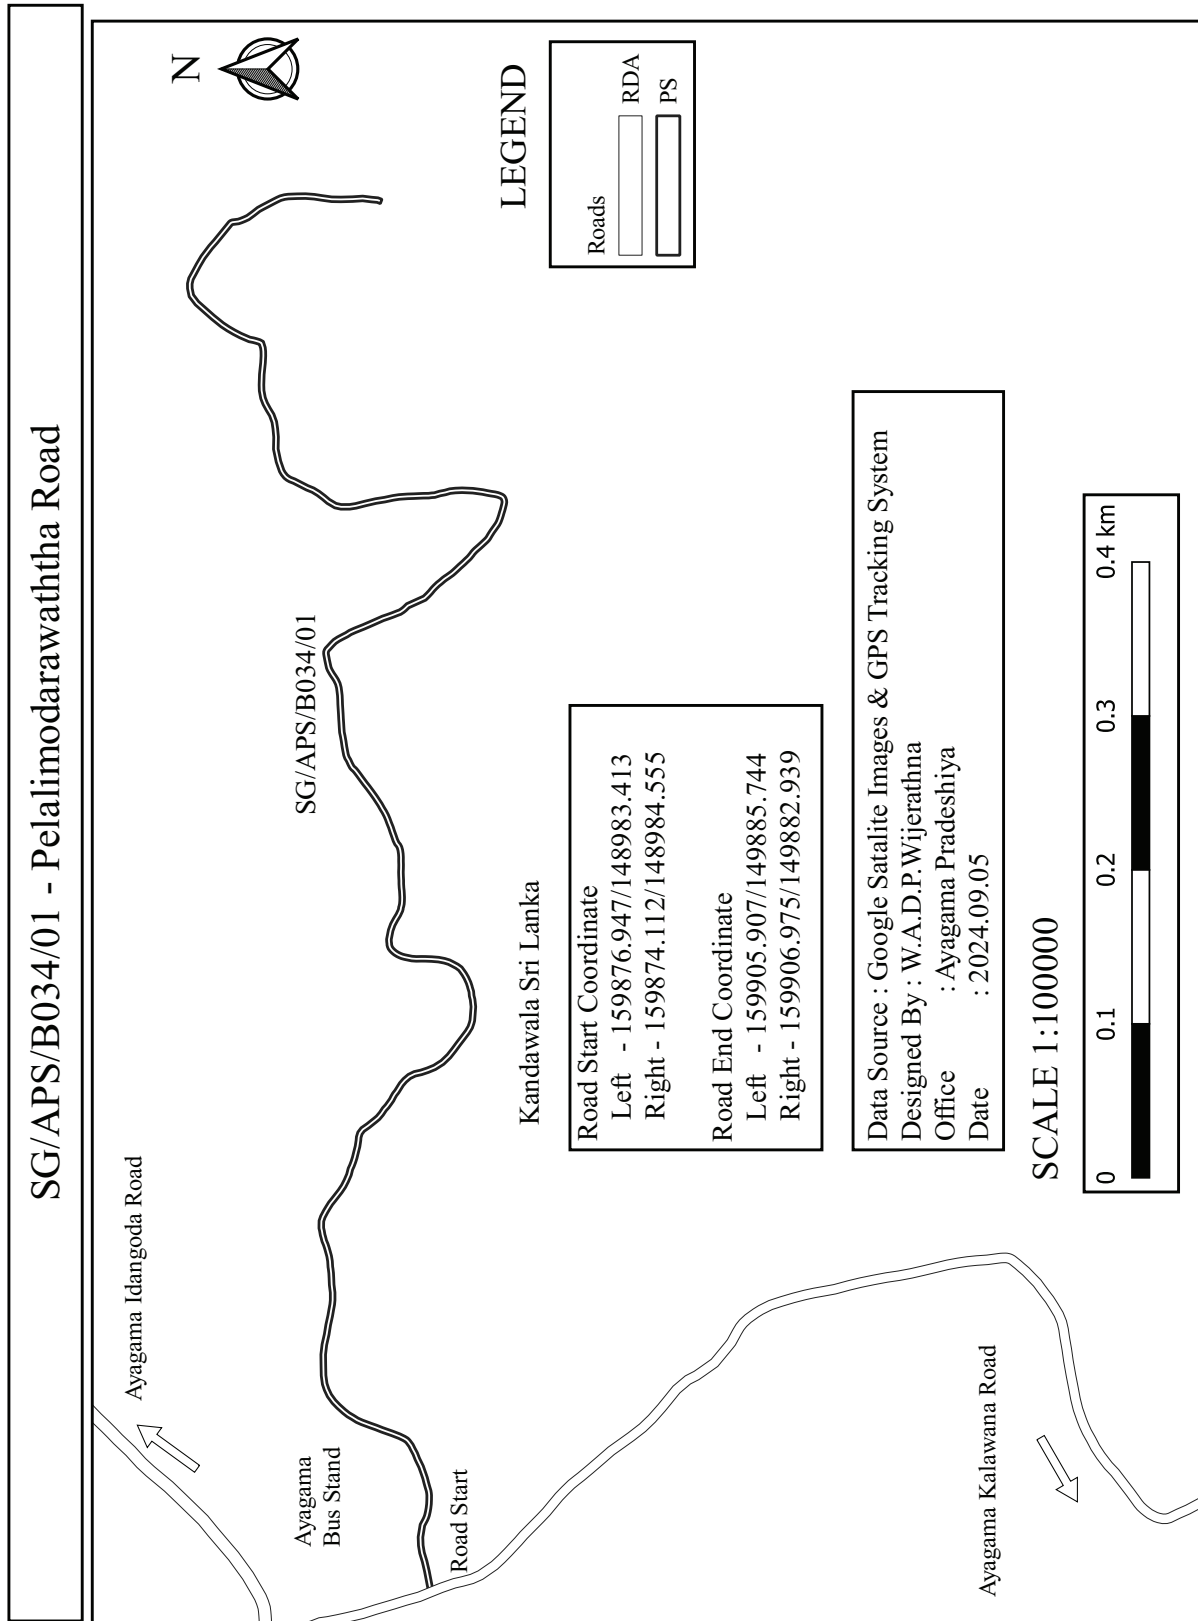

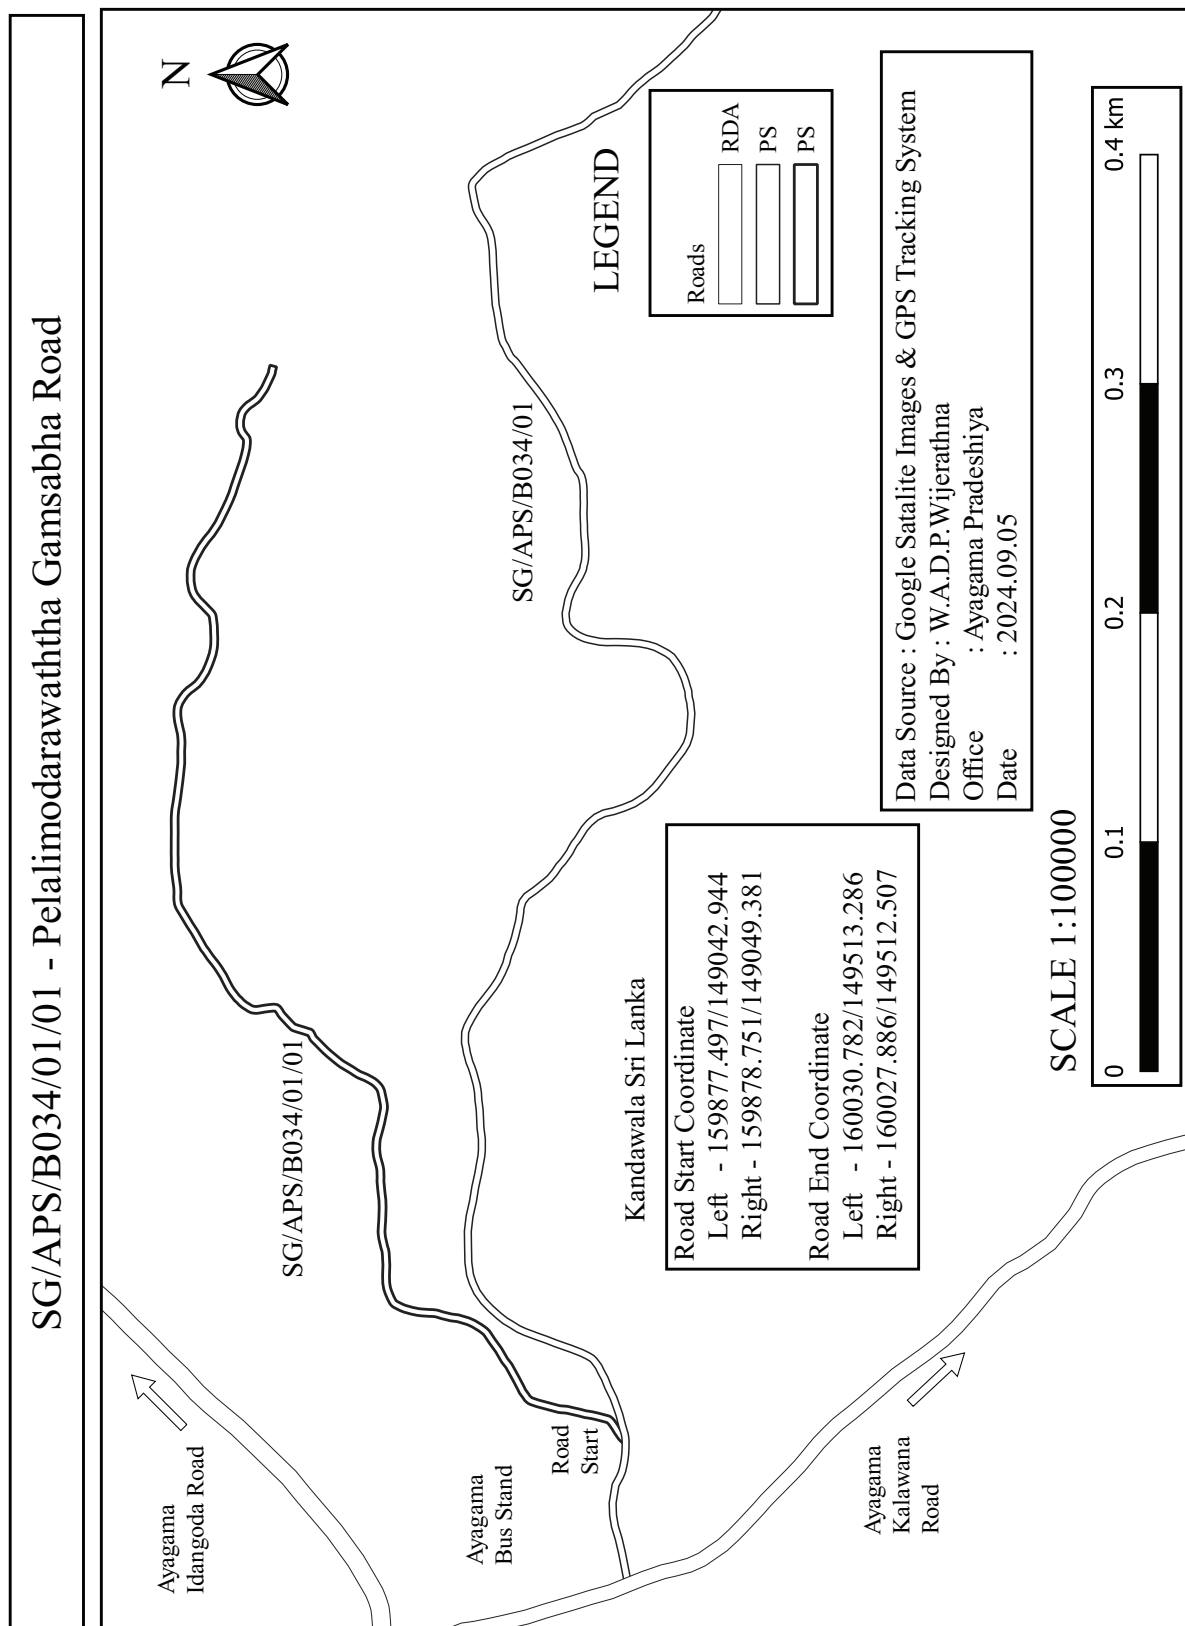

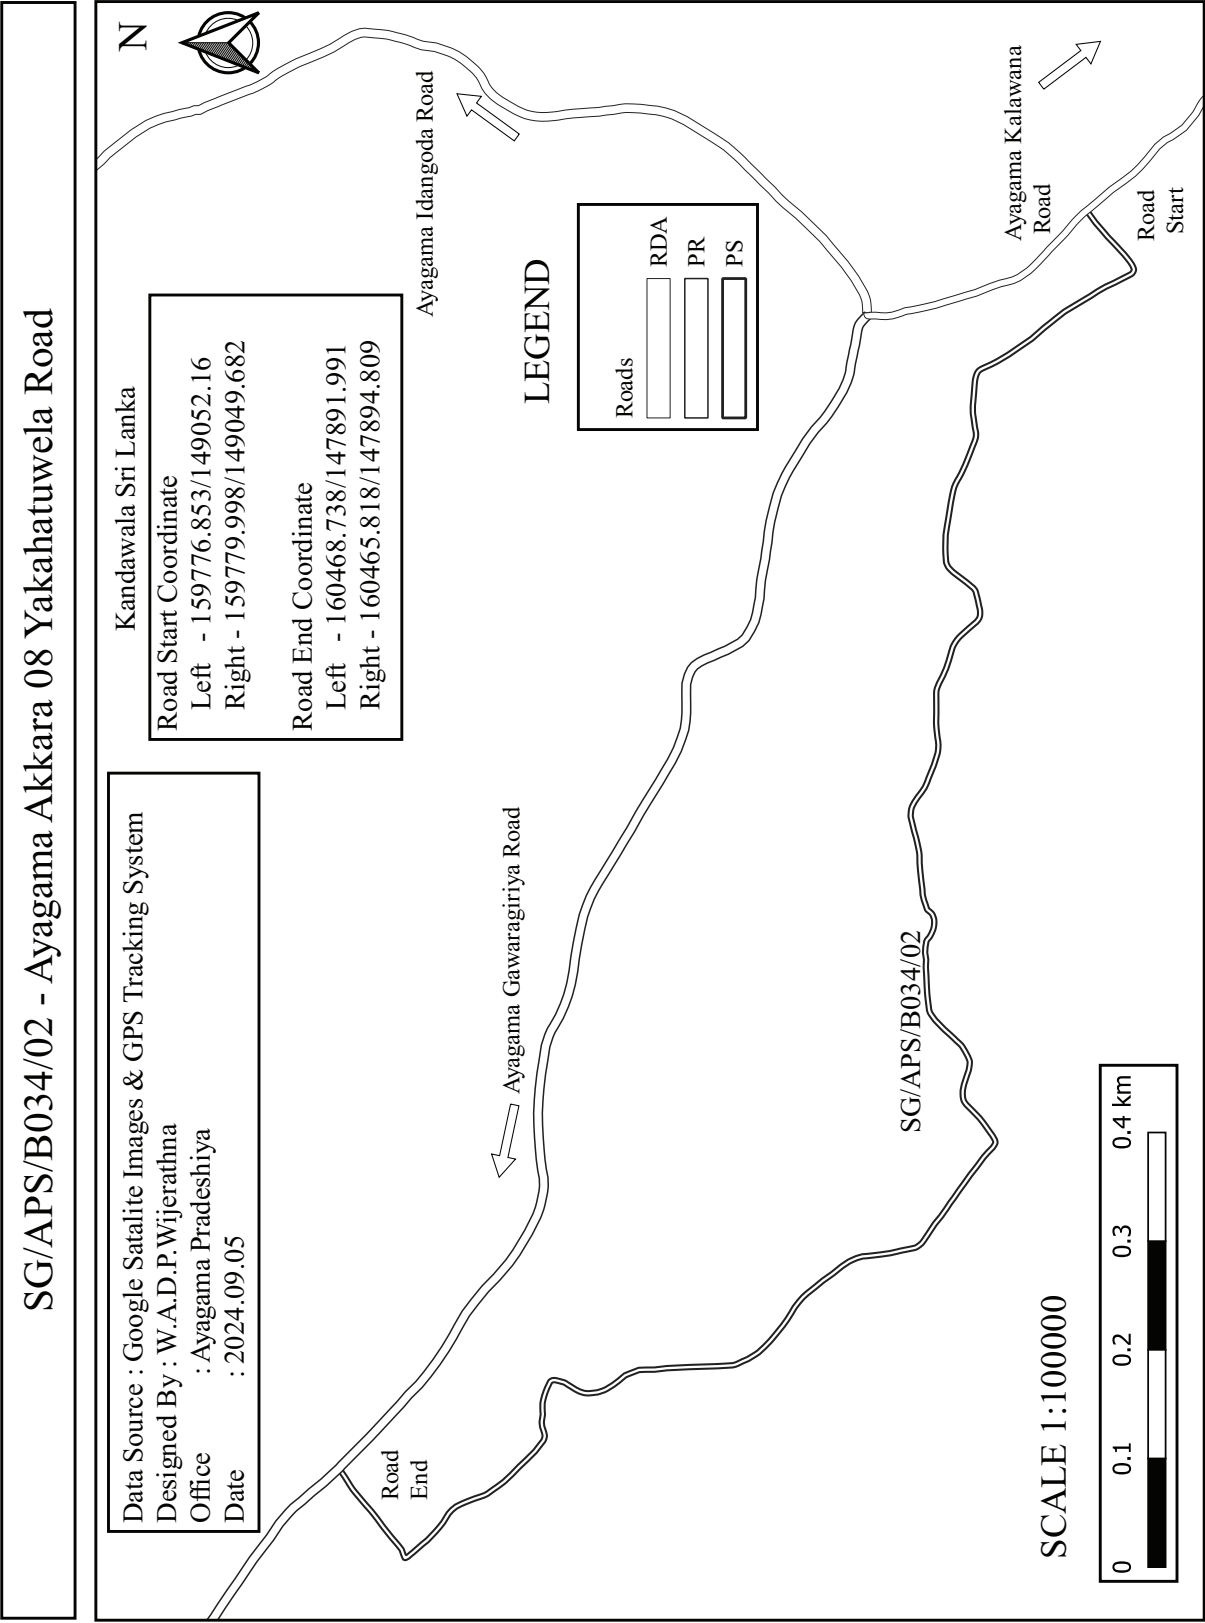


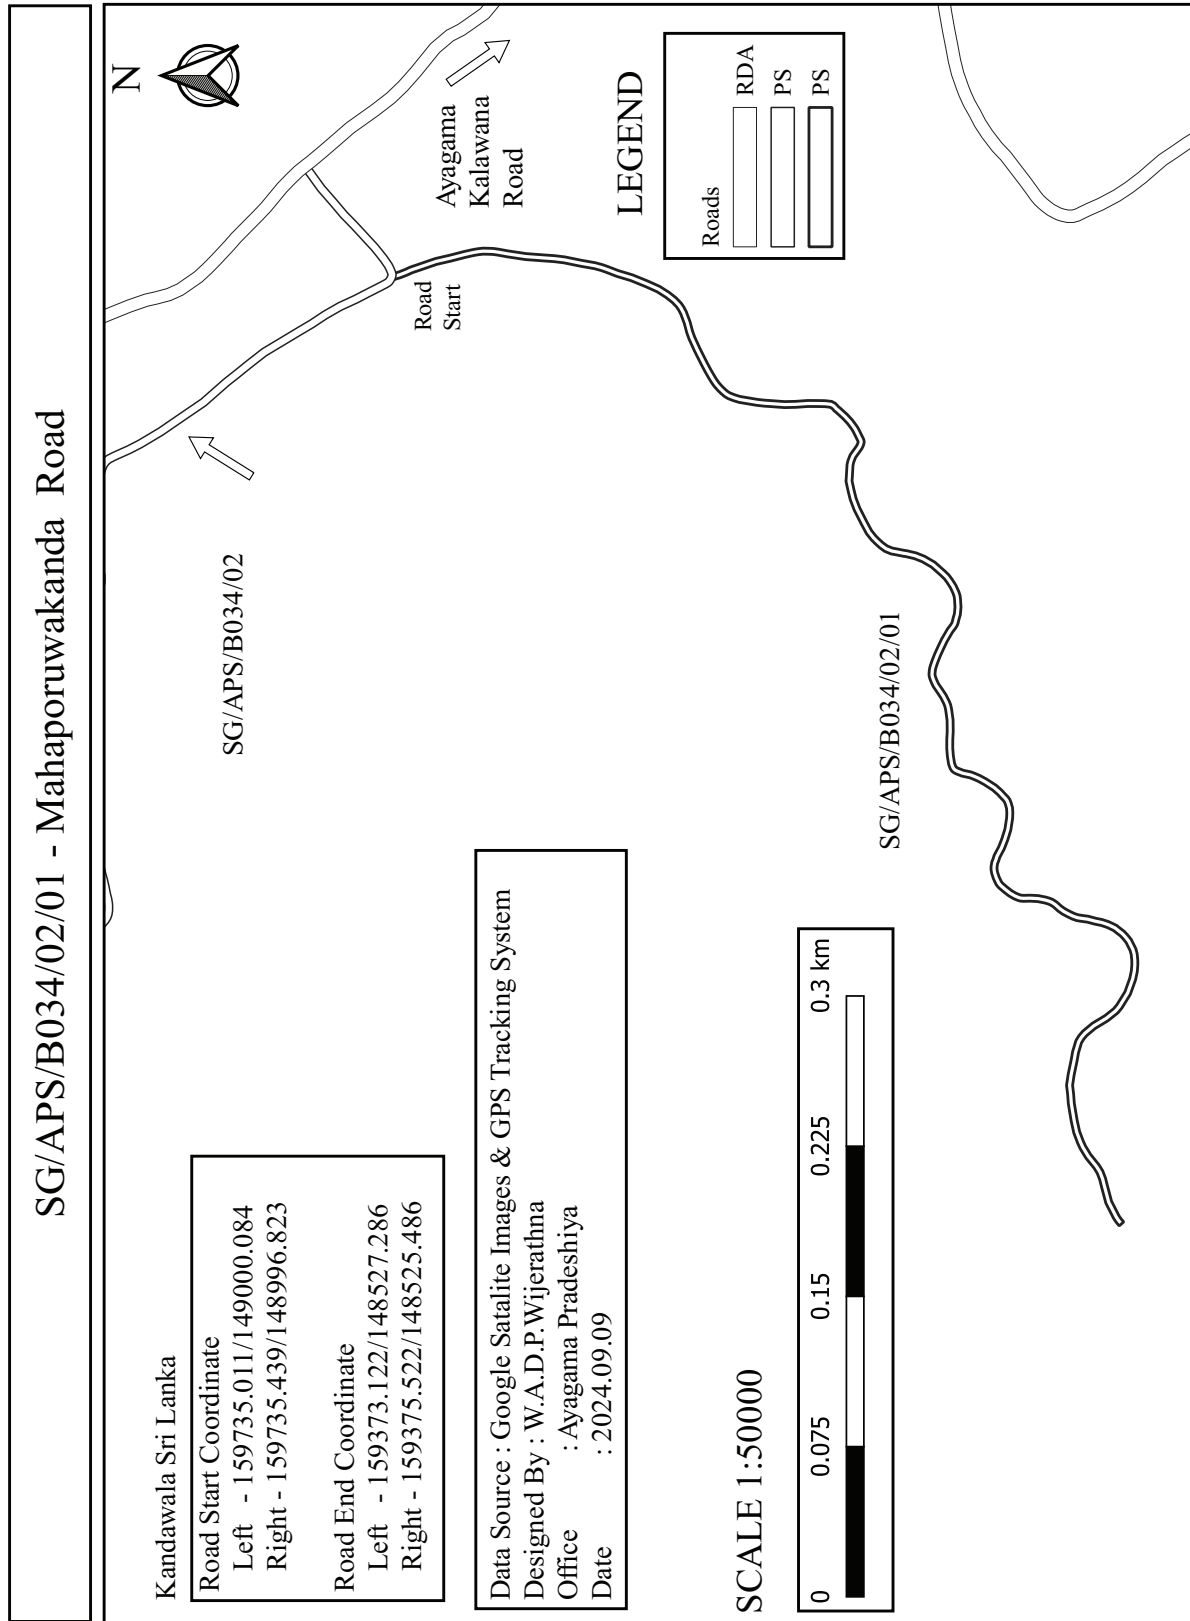


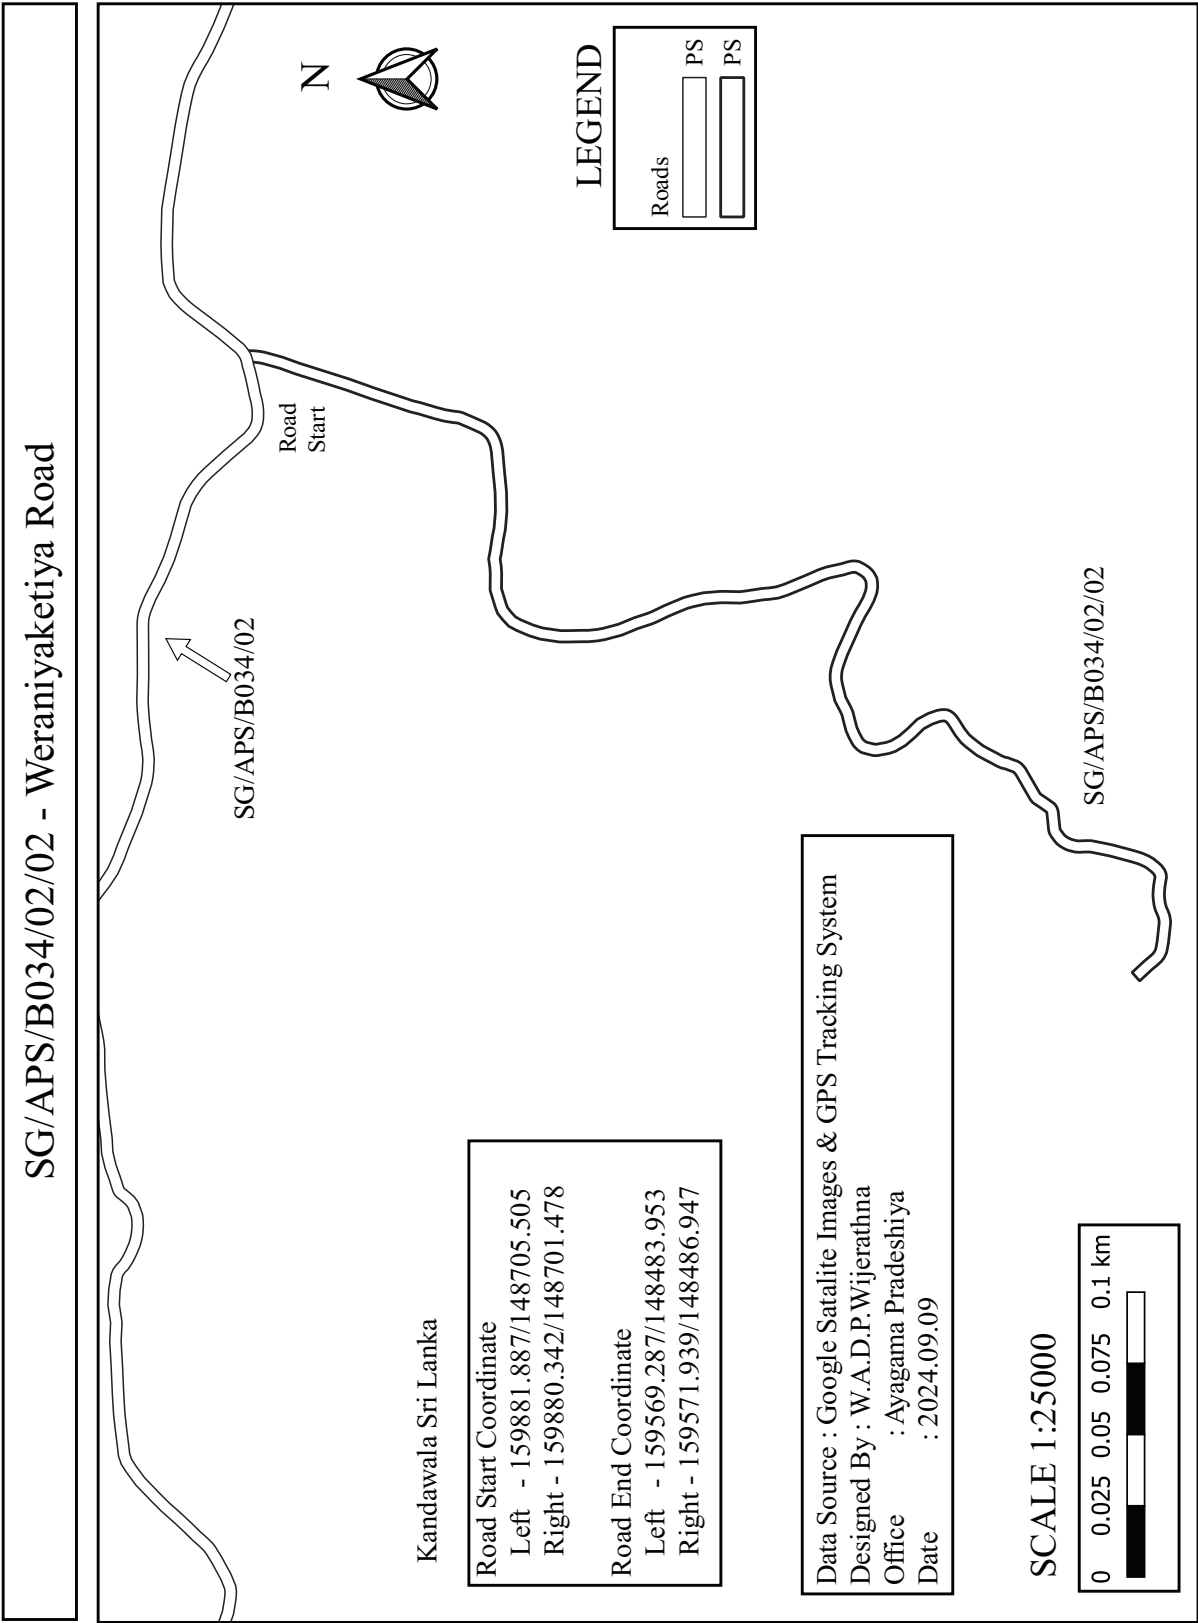





SG/APS/B034/02/02/01 - First Lane of Weraniyaketiya Road

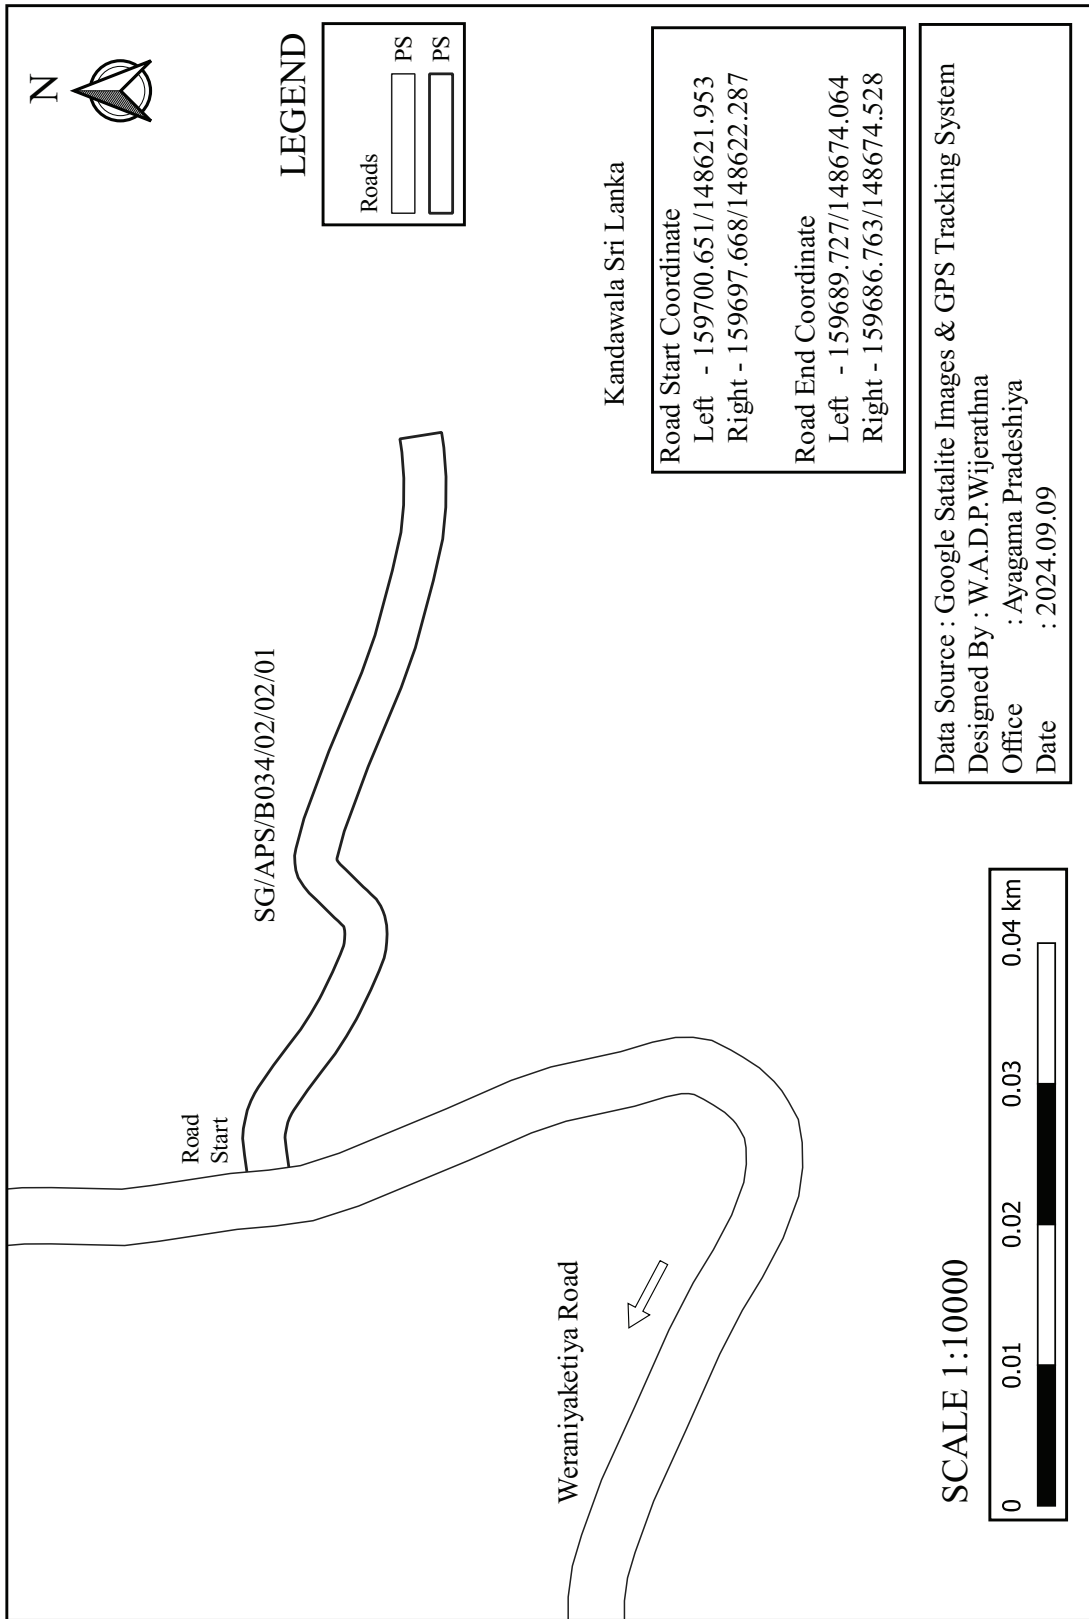


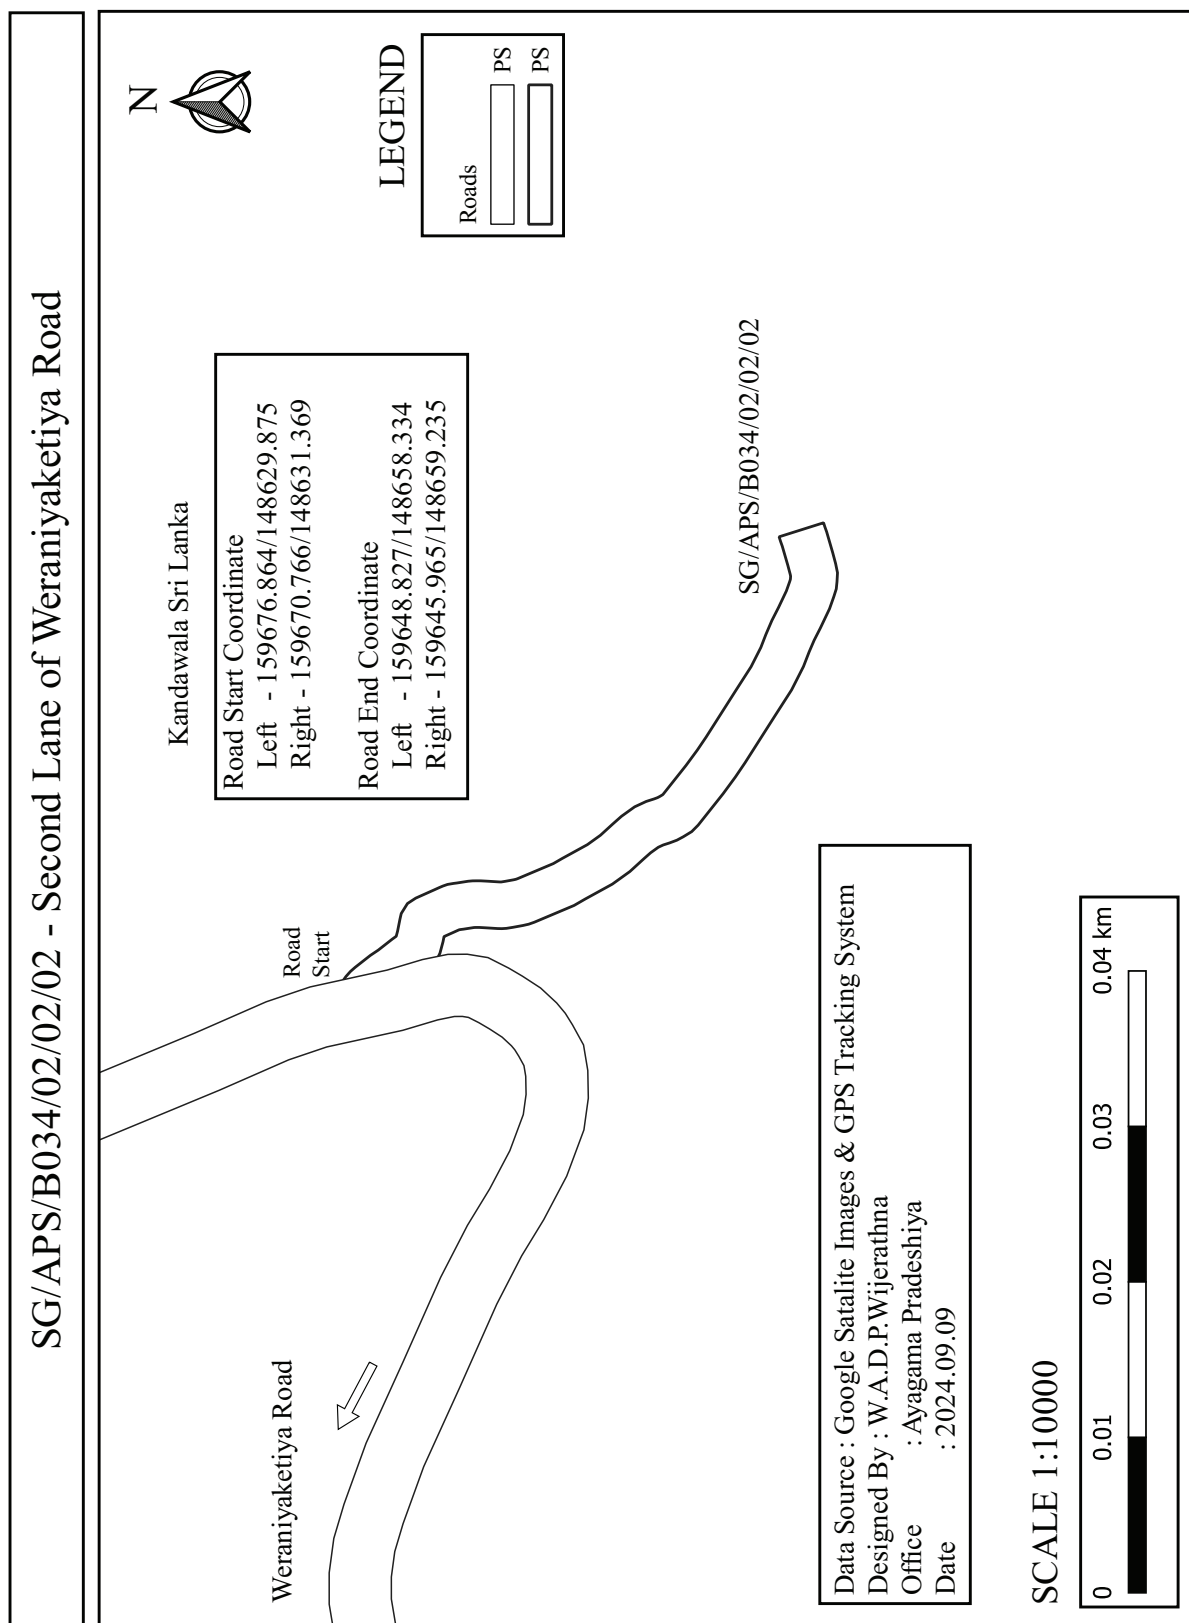


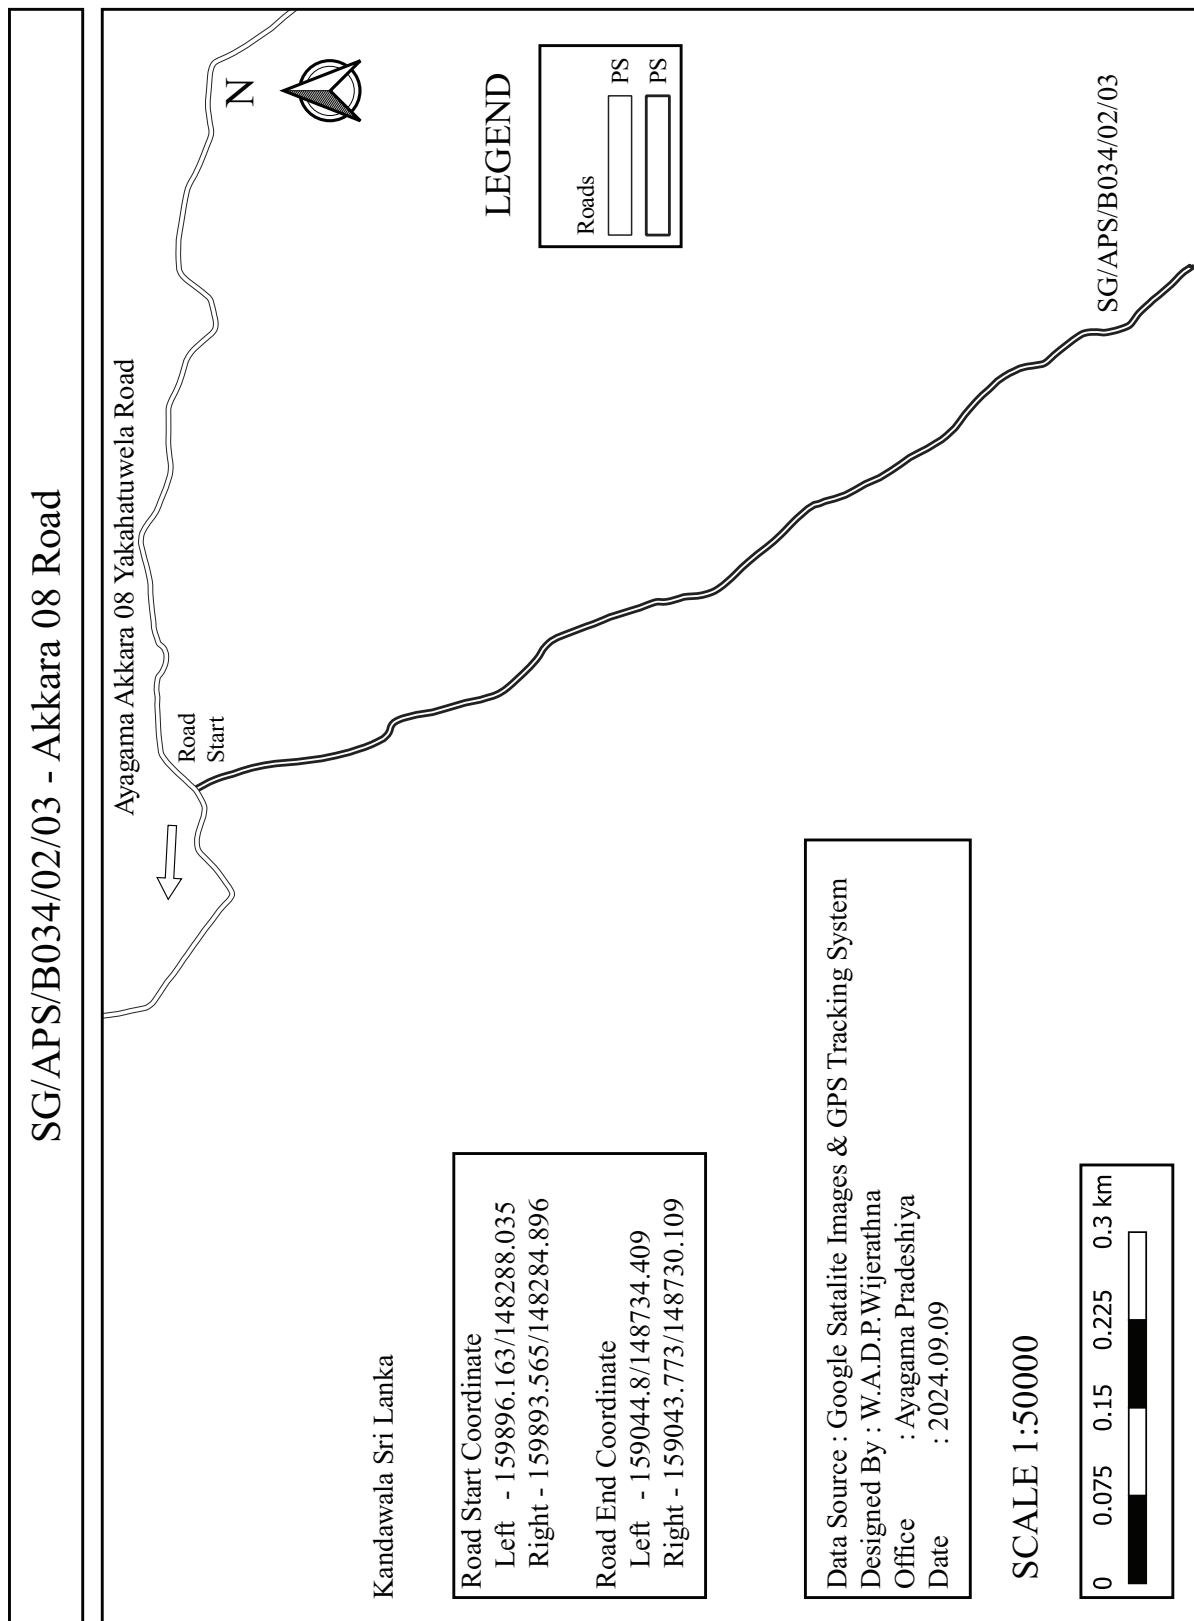



Data Source : Google Satalite Images & GPS Tracking System  
 Designed By : W.A.D.P.Wijerathna  
 Office : Ayagama Pradeshiya  
 Date : 2024.09.09

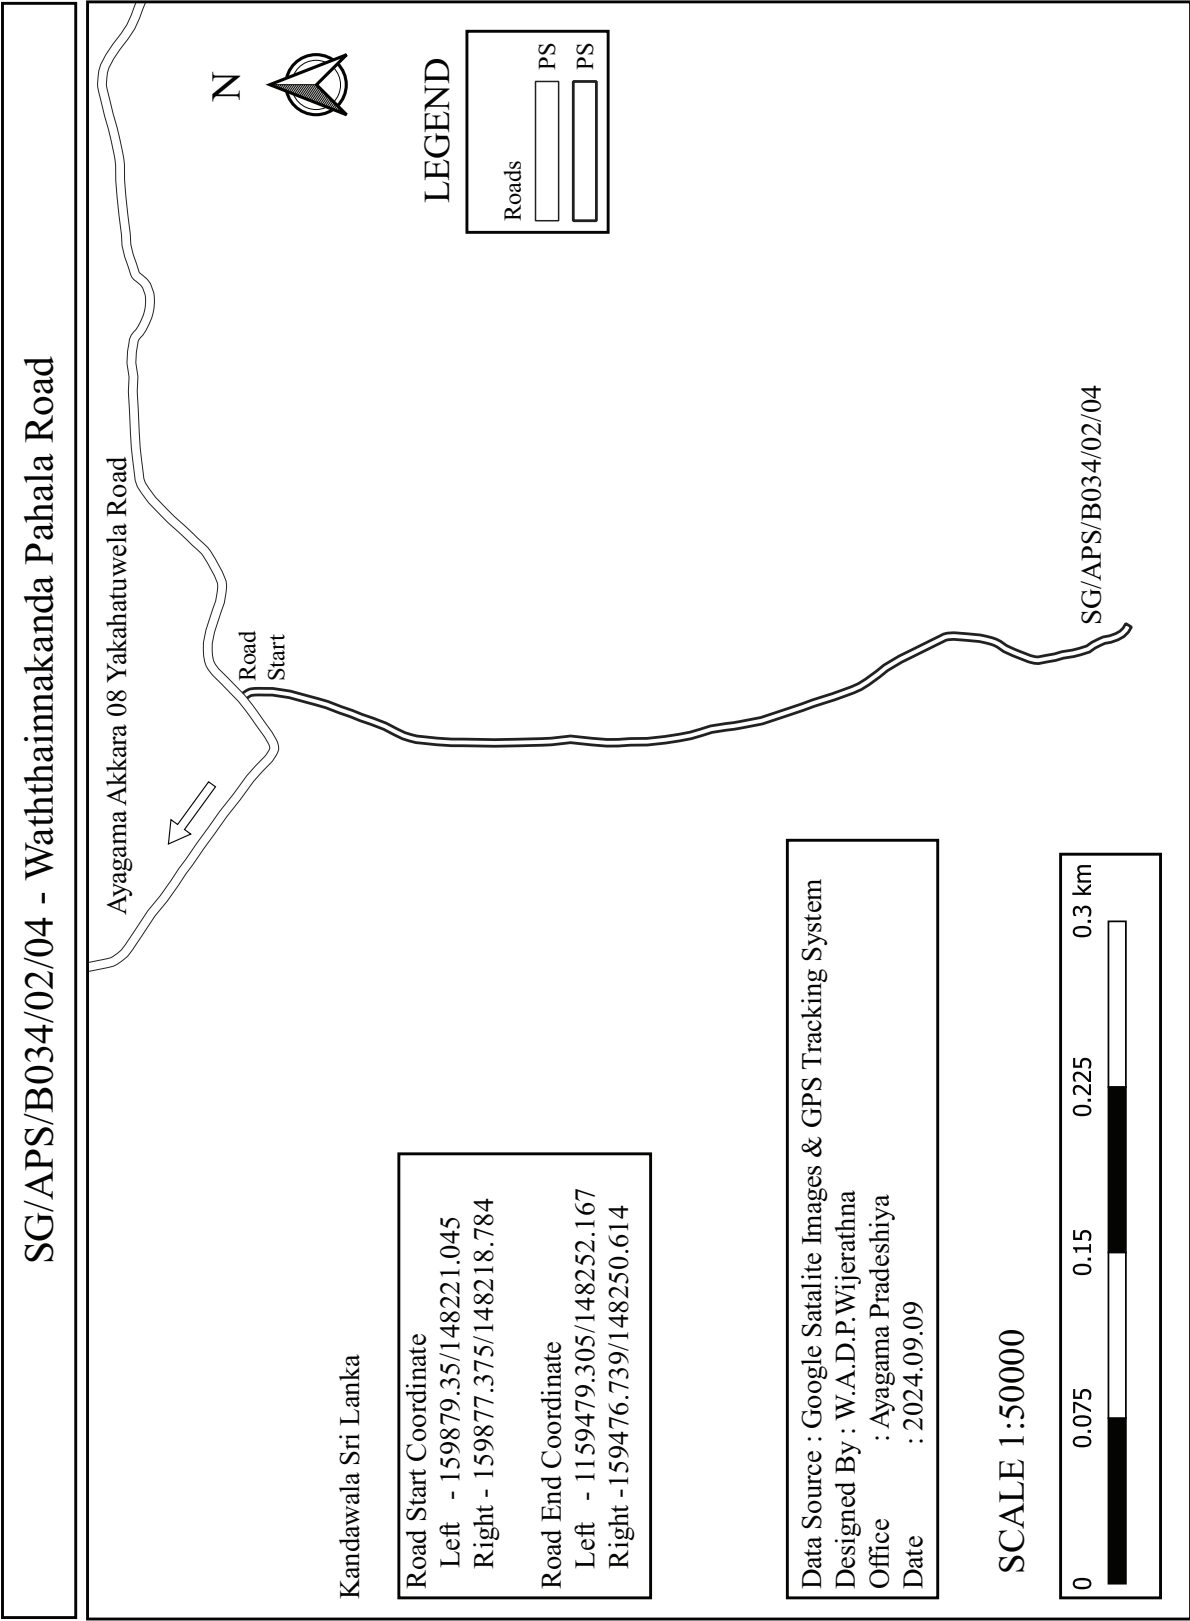

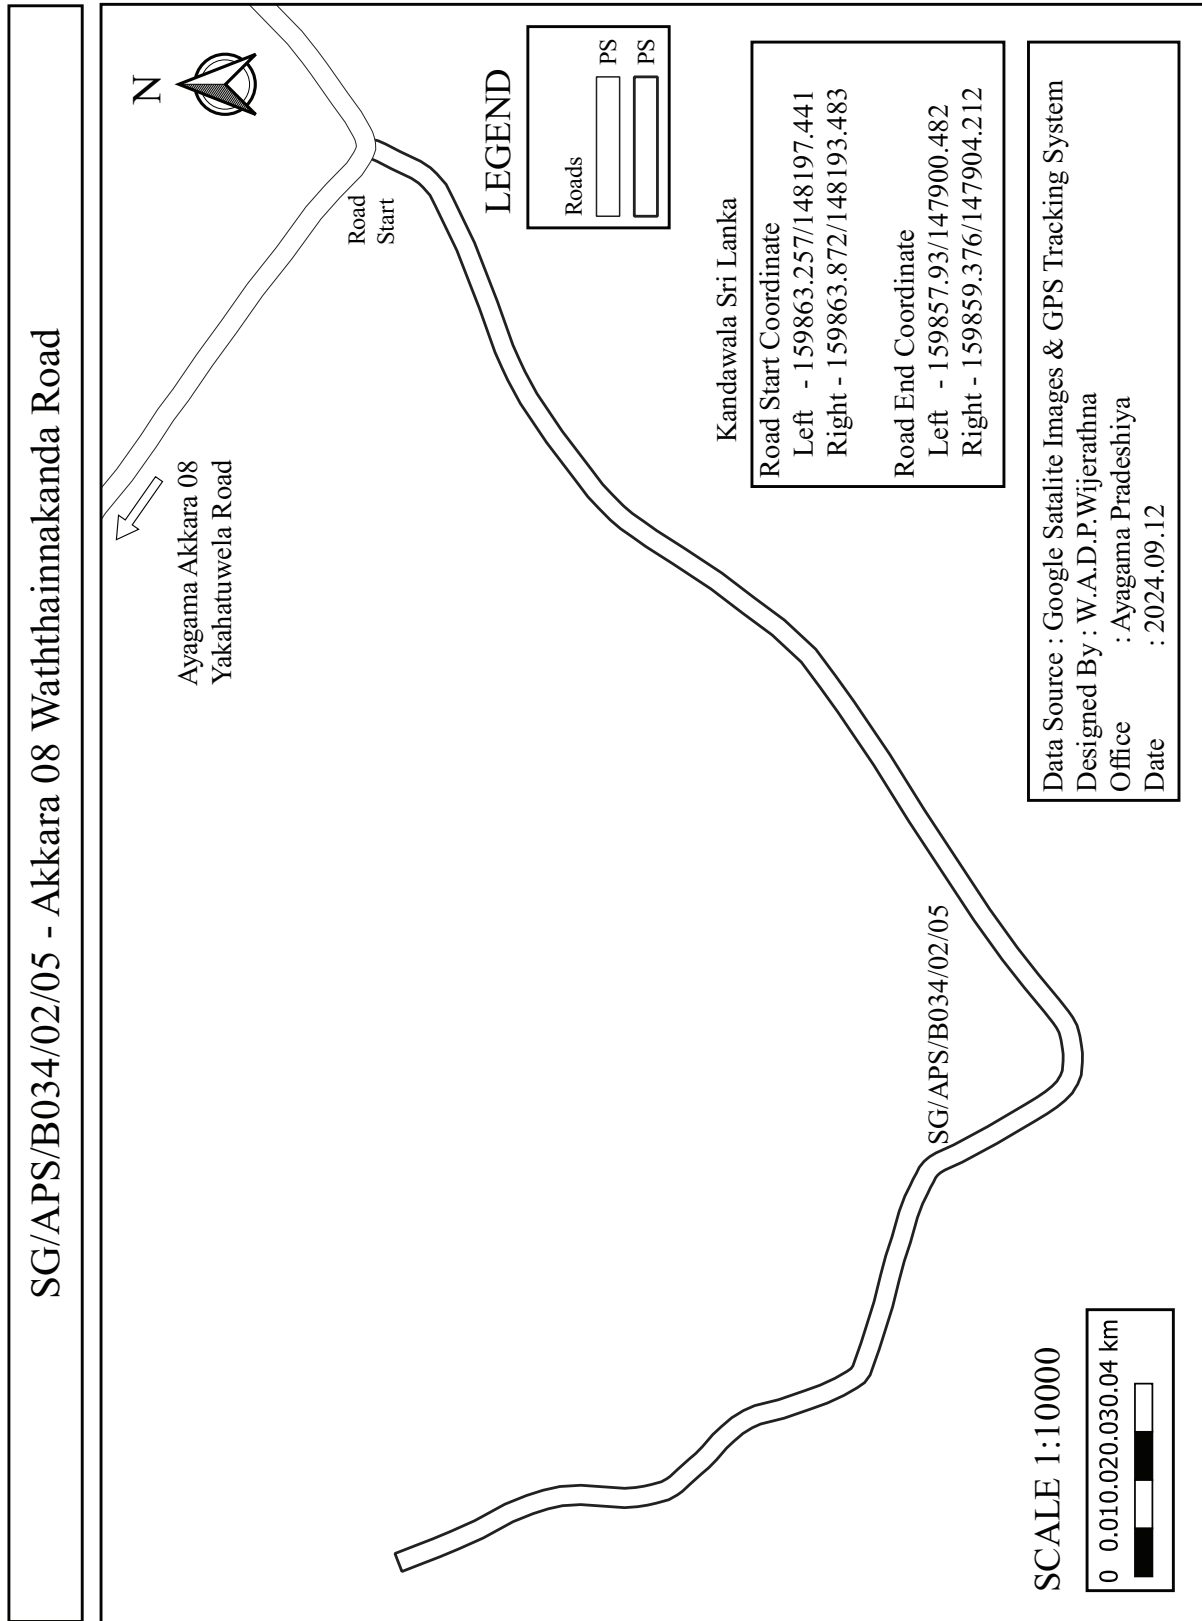


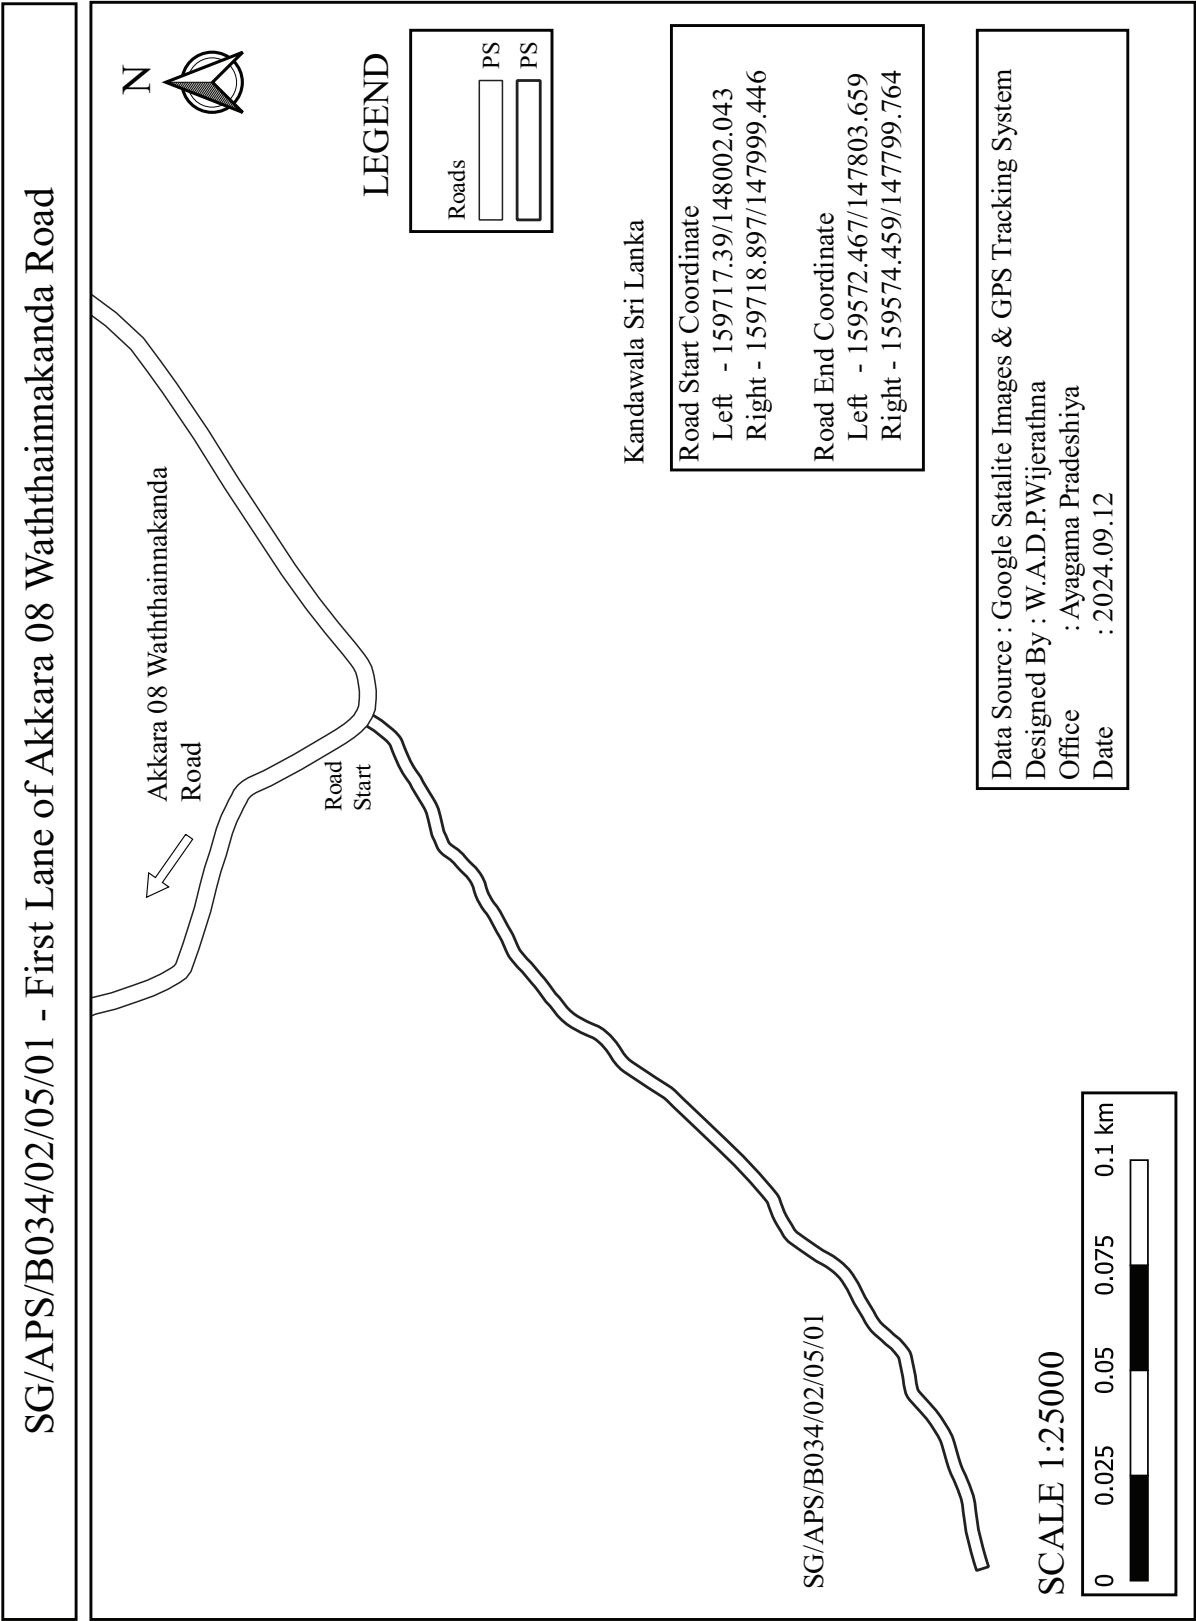

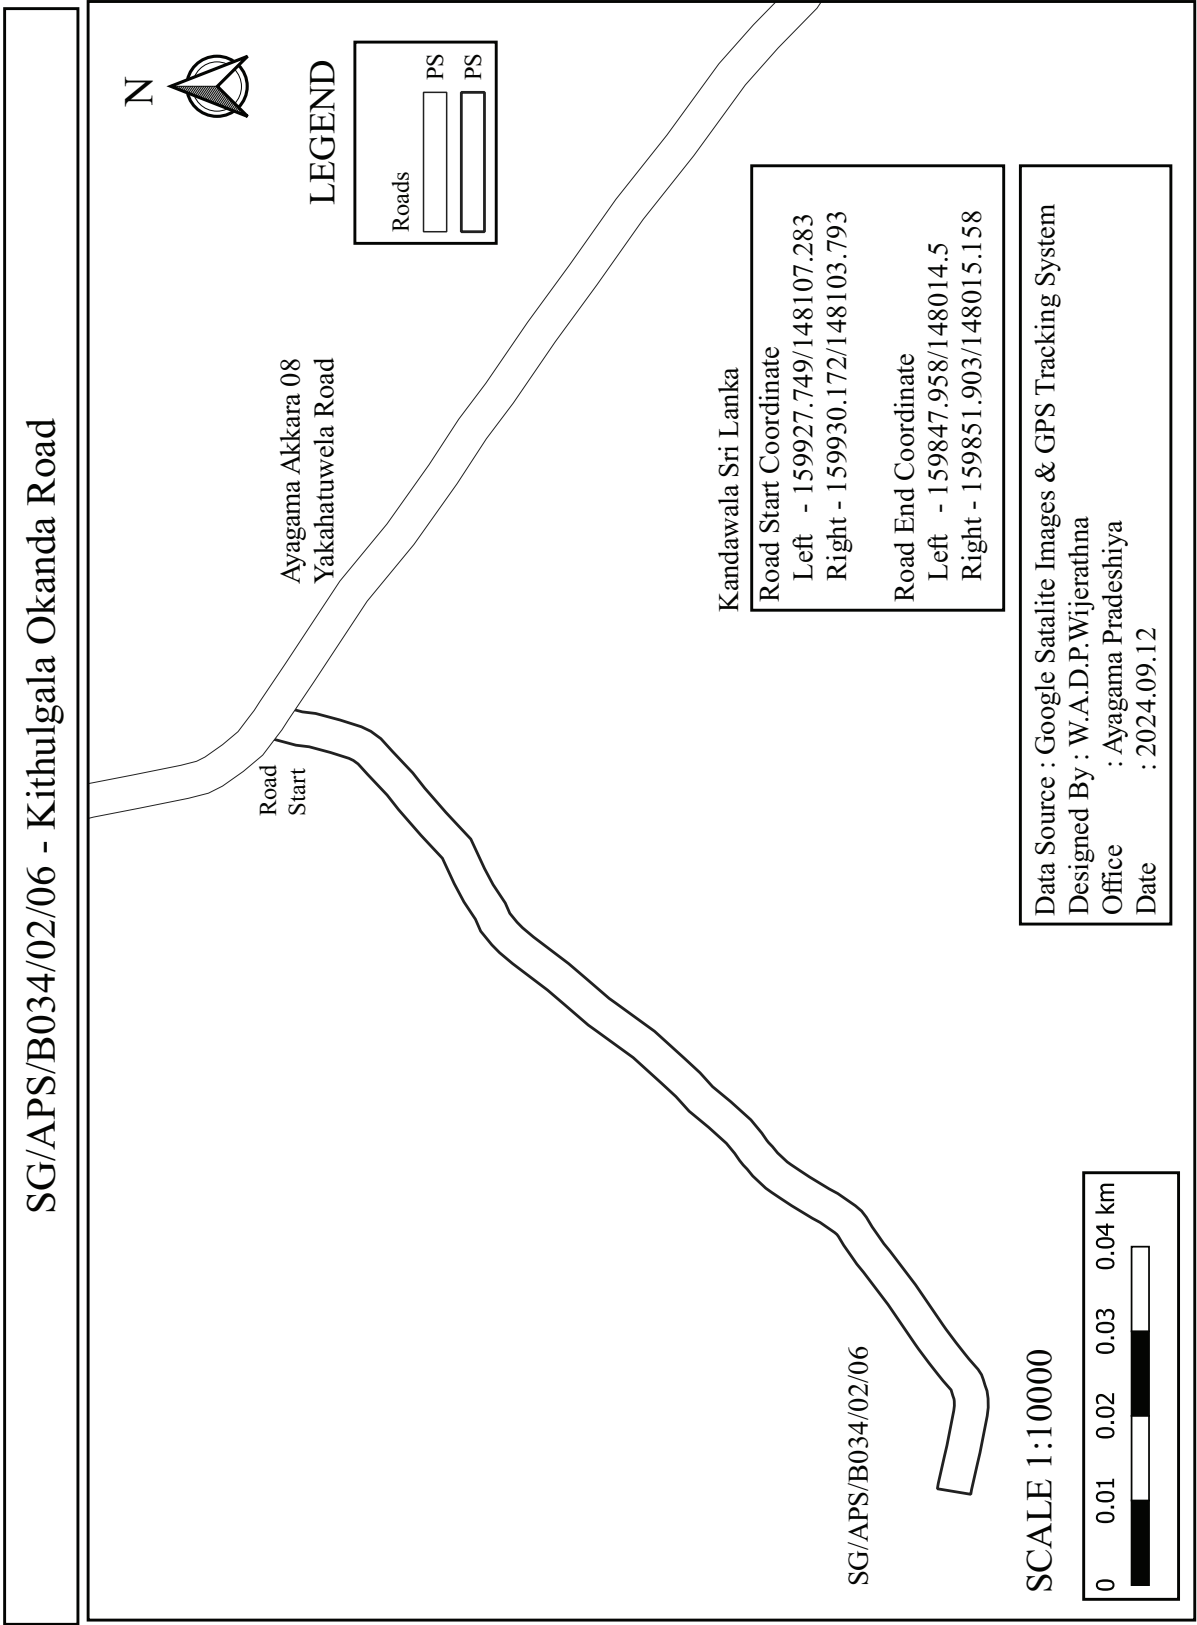

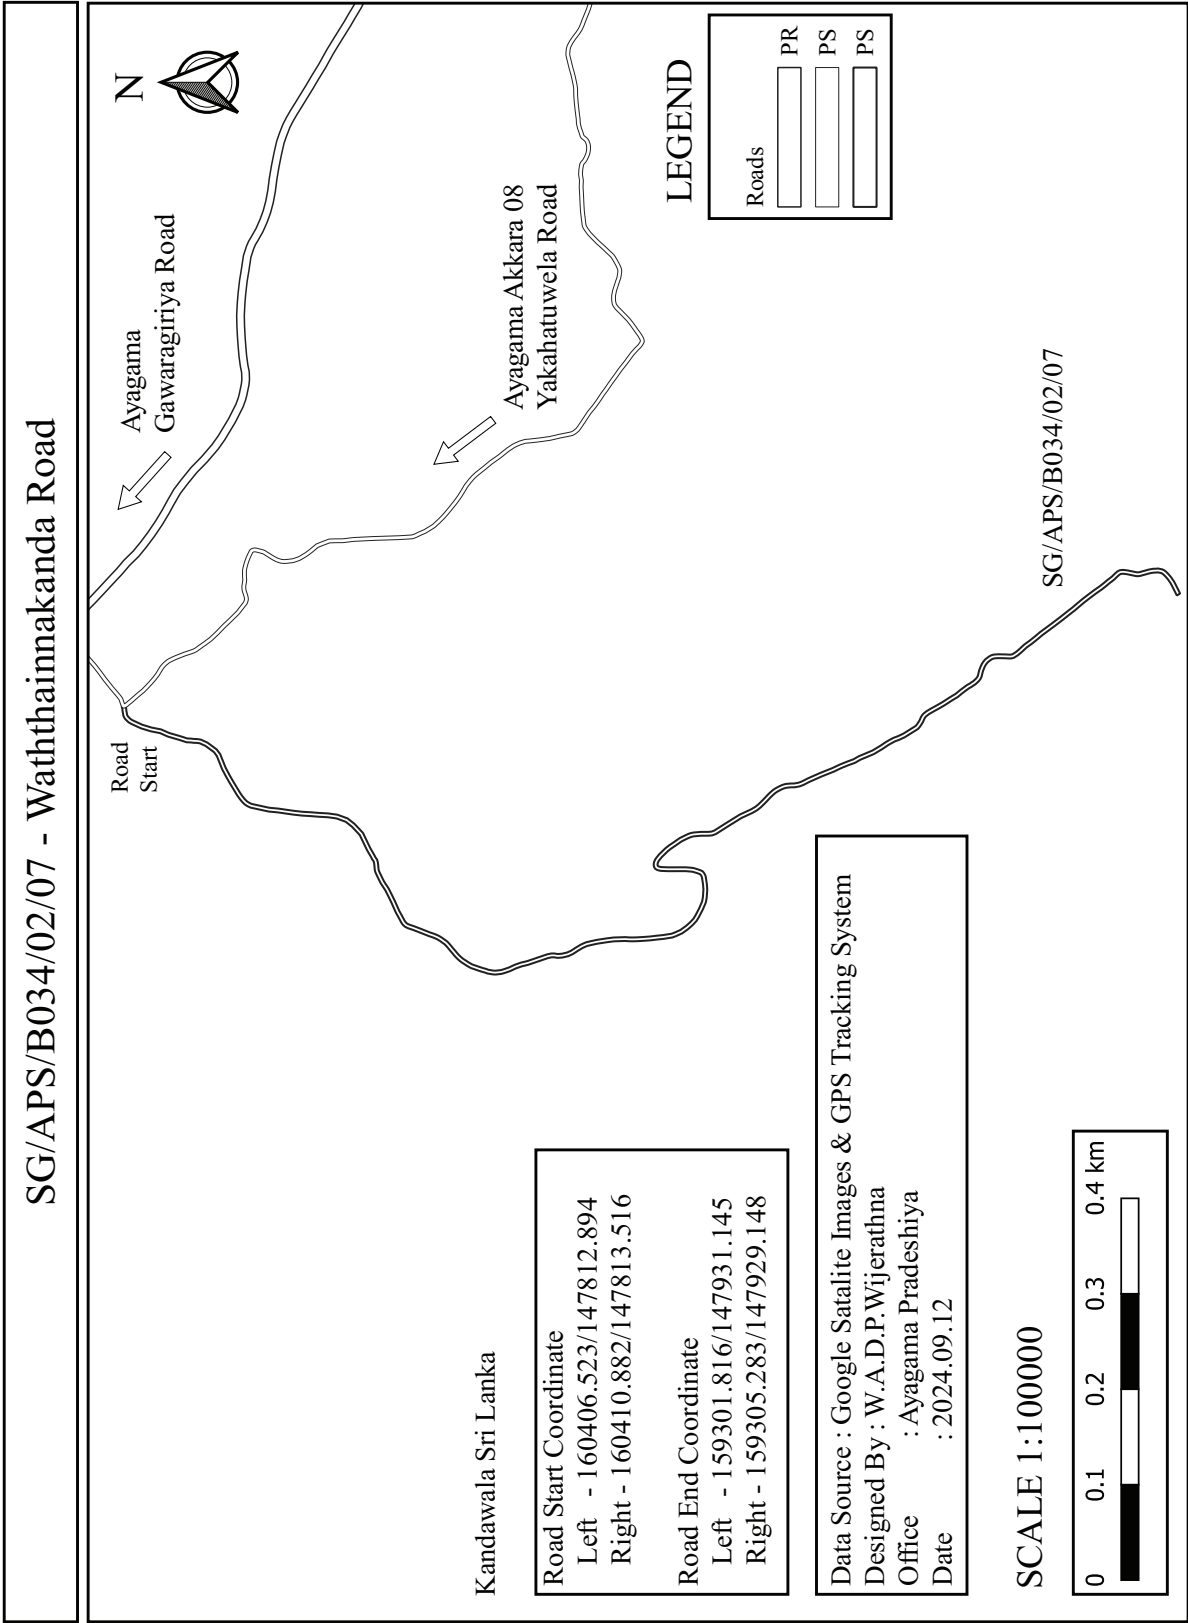




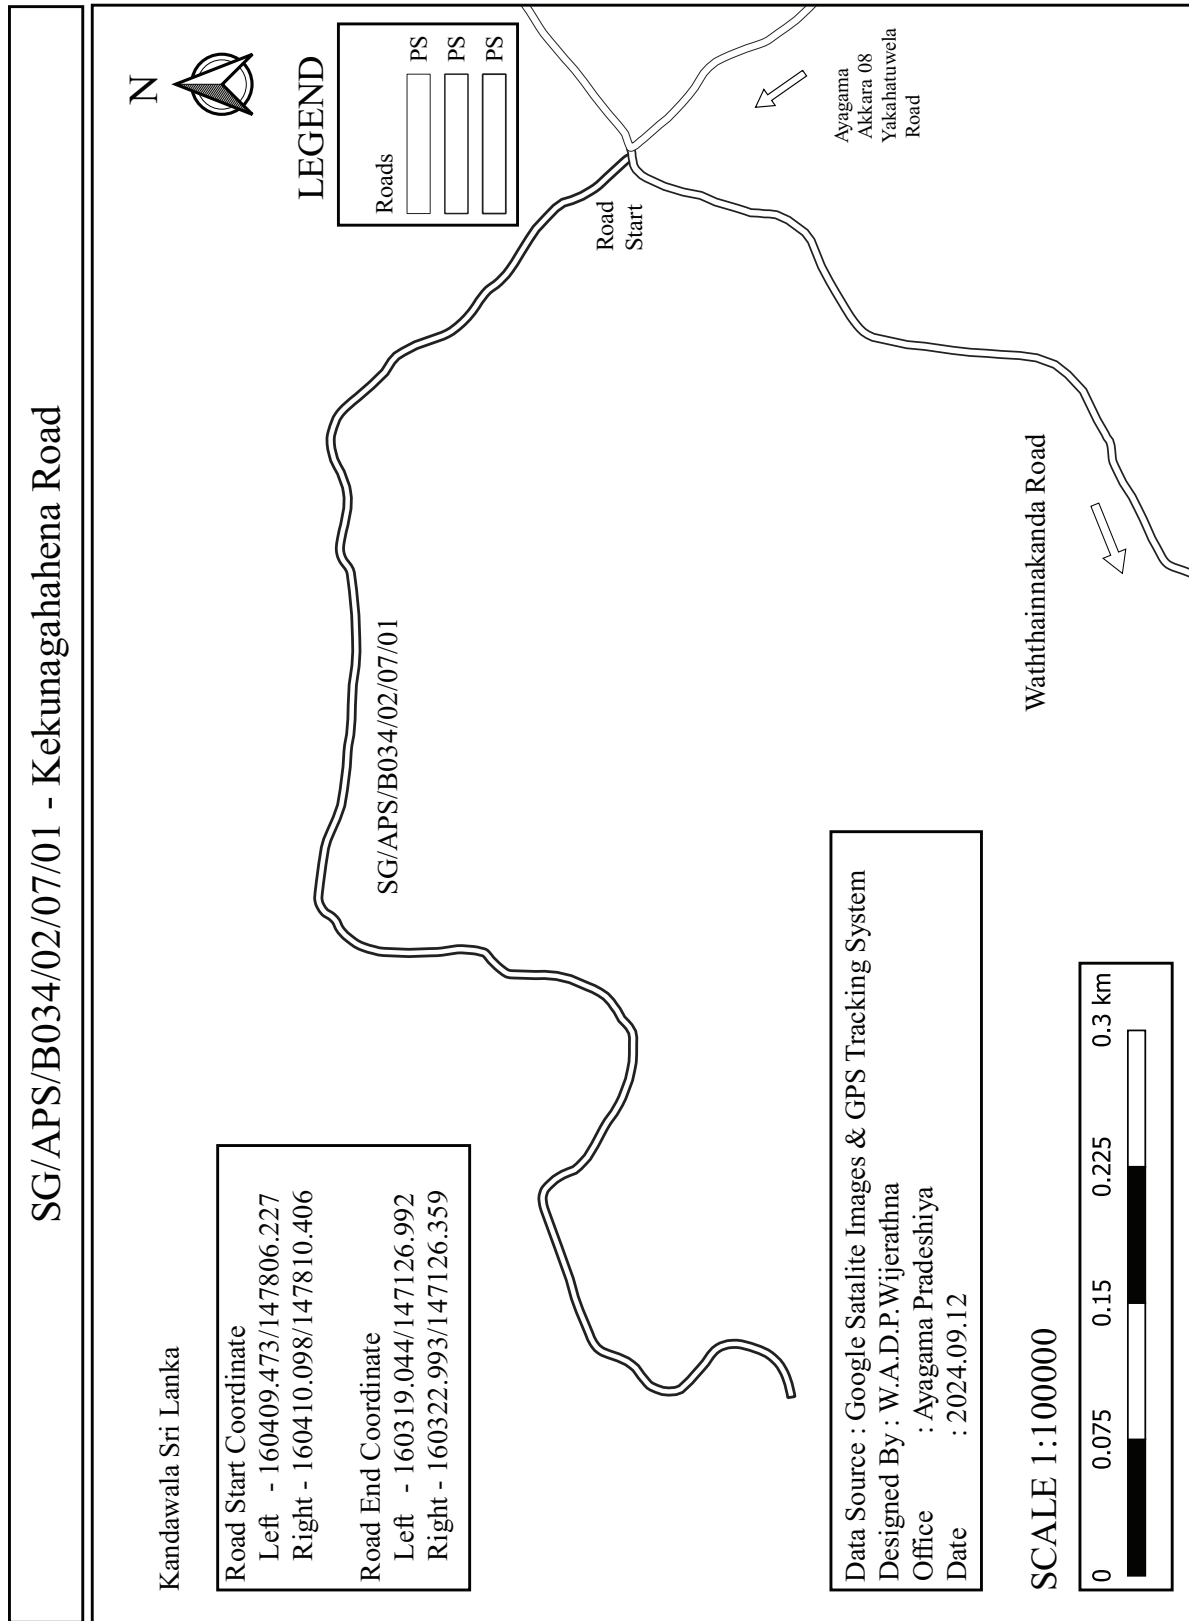


Data Source : Google Satalite Images & GPS Tracking System  
 Designed By : W.A.D.P.Wijerathna  
 Office : Ayagama Pradeshiya  
 Date : 2024.09.12


**SCALE 1:100000**

0    0.075    0.15    0.225    0.3 km

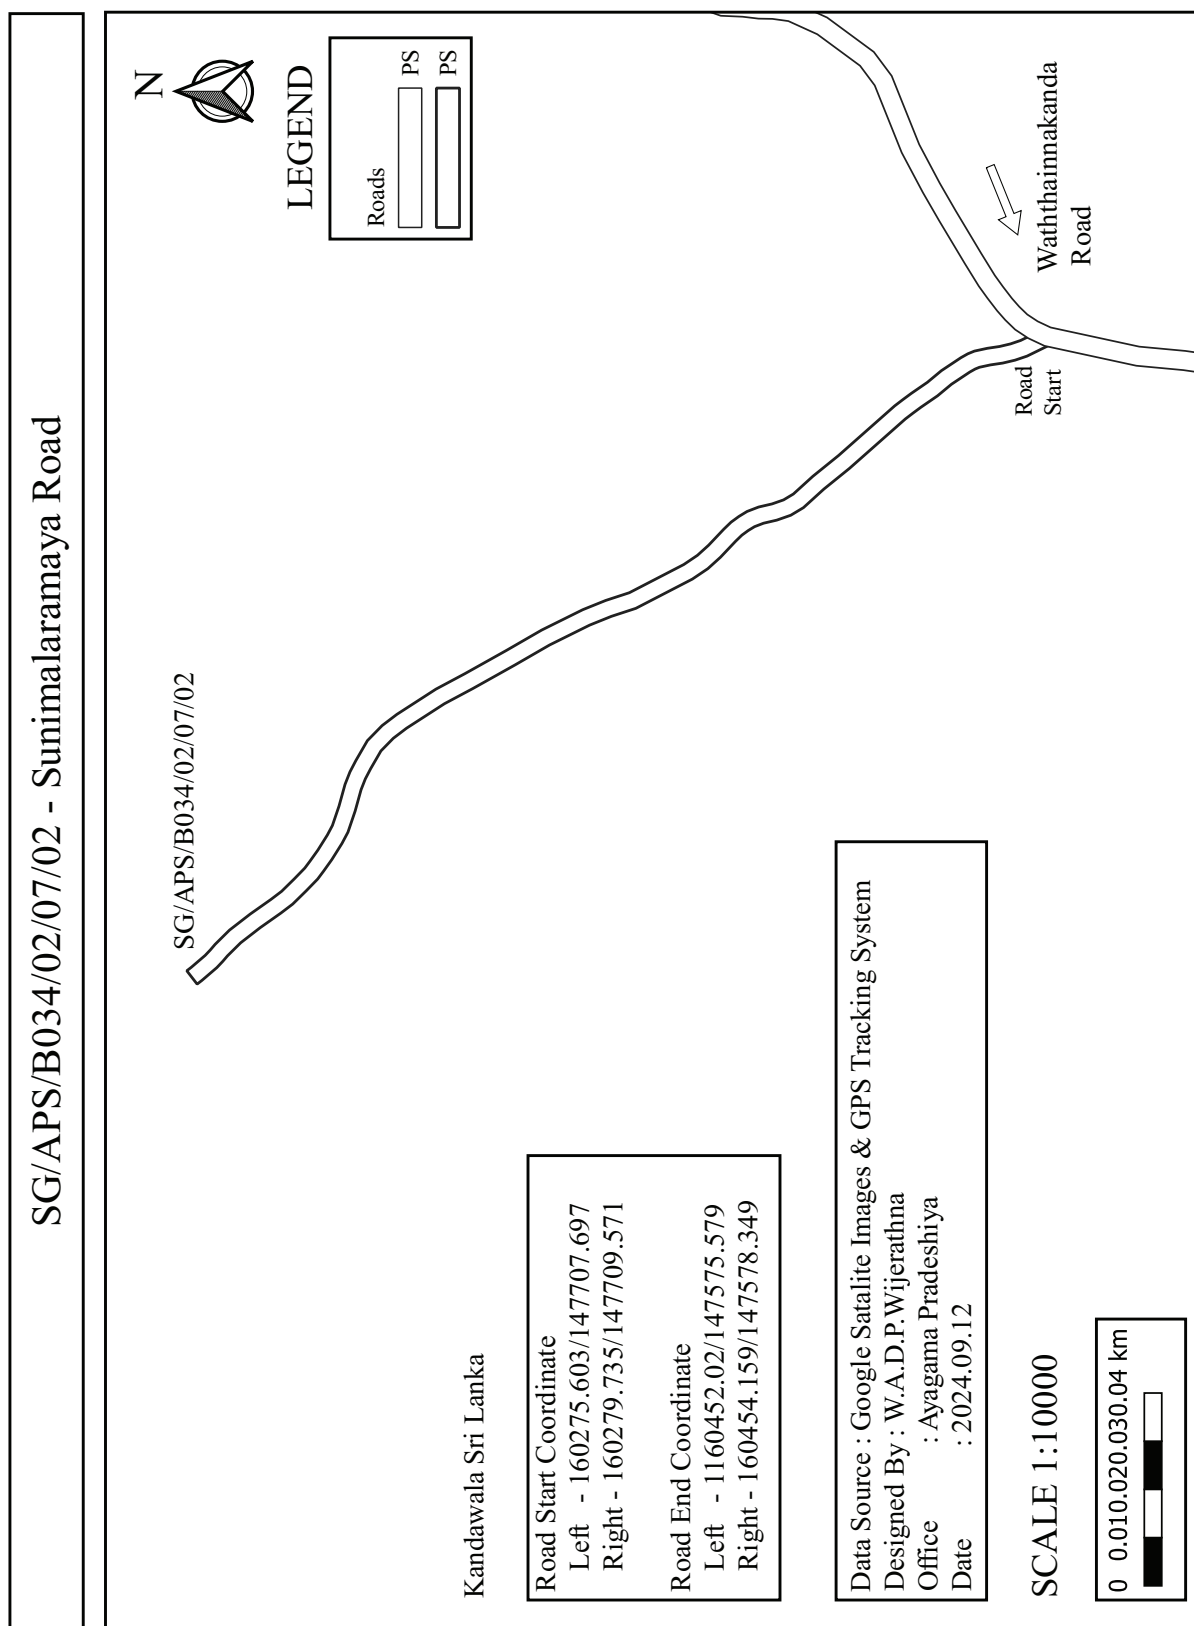



## SG/APS/B034/02/07/03 - First Lane of Waththainnakanda Road

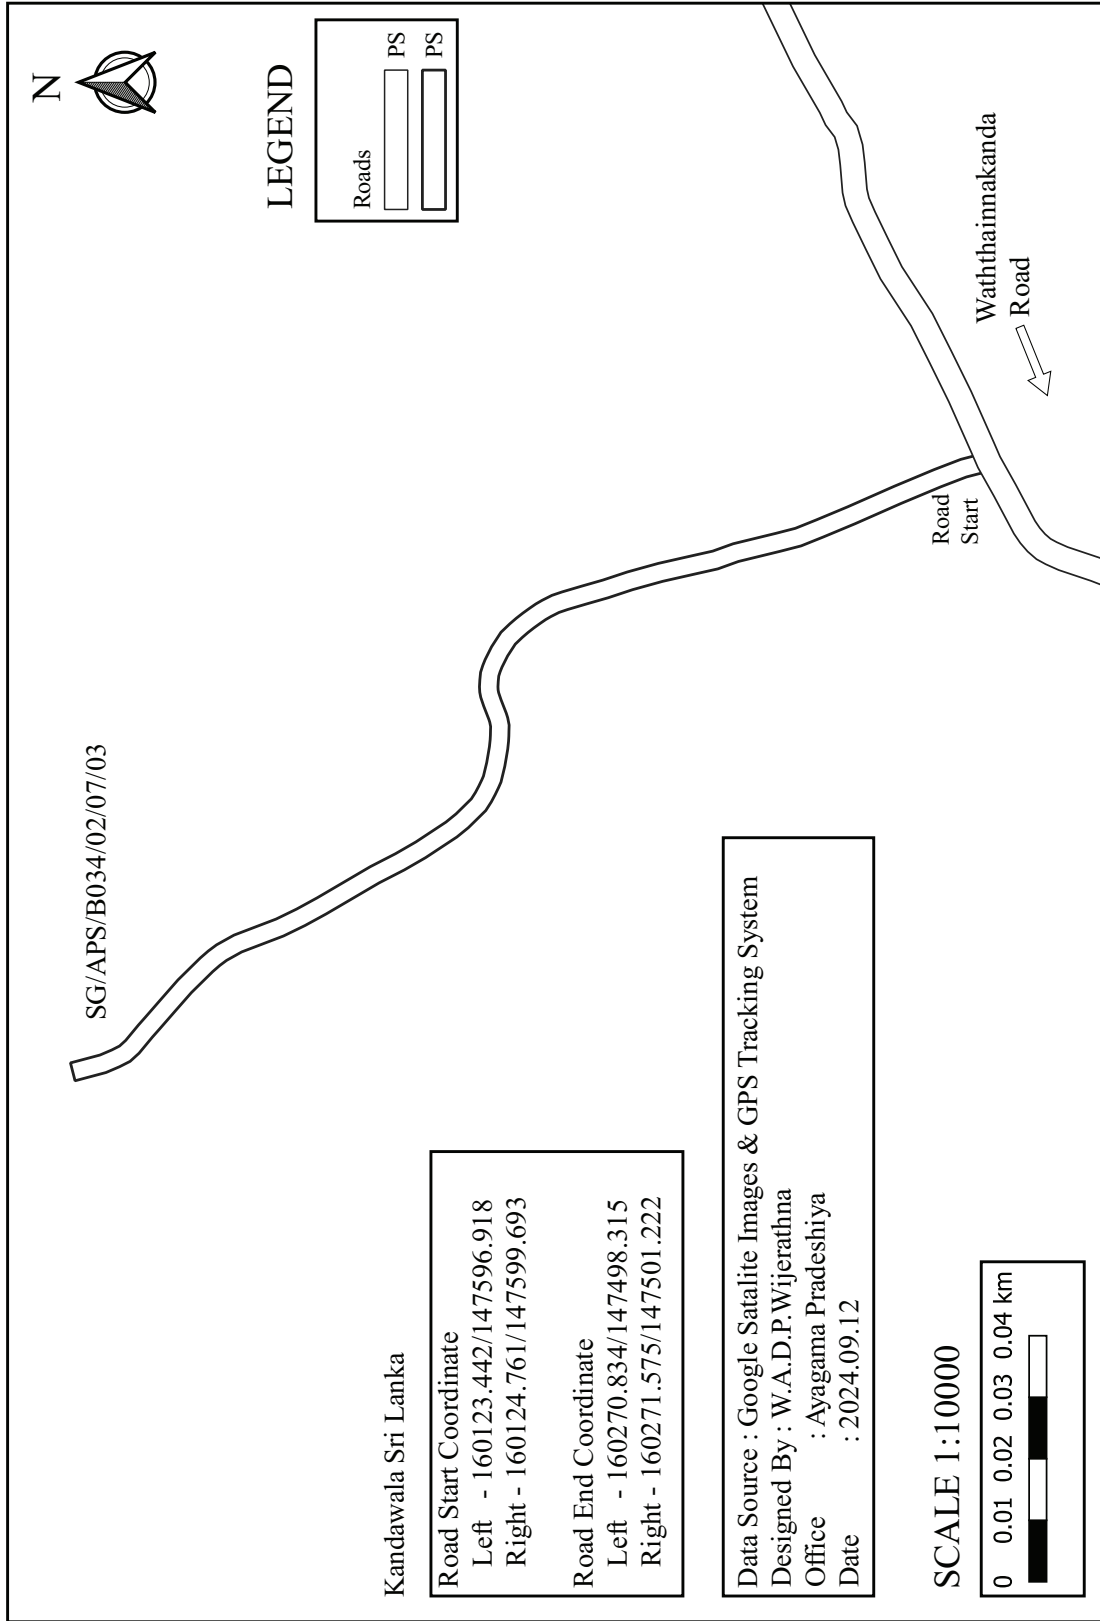


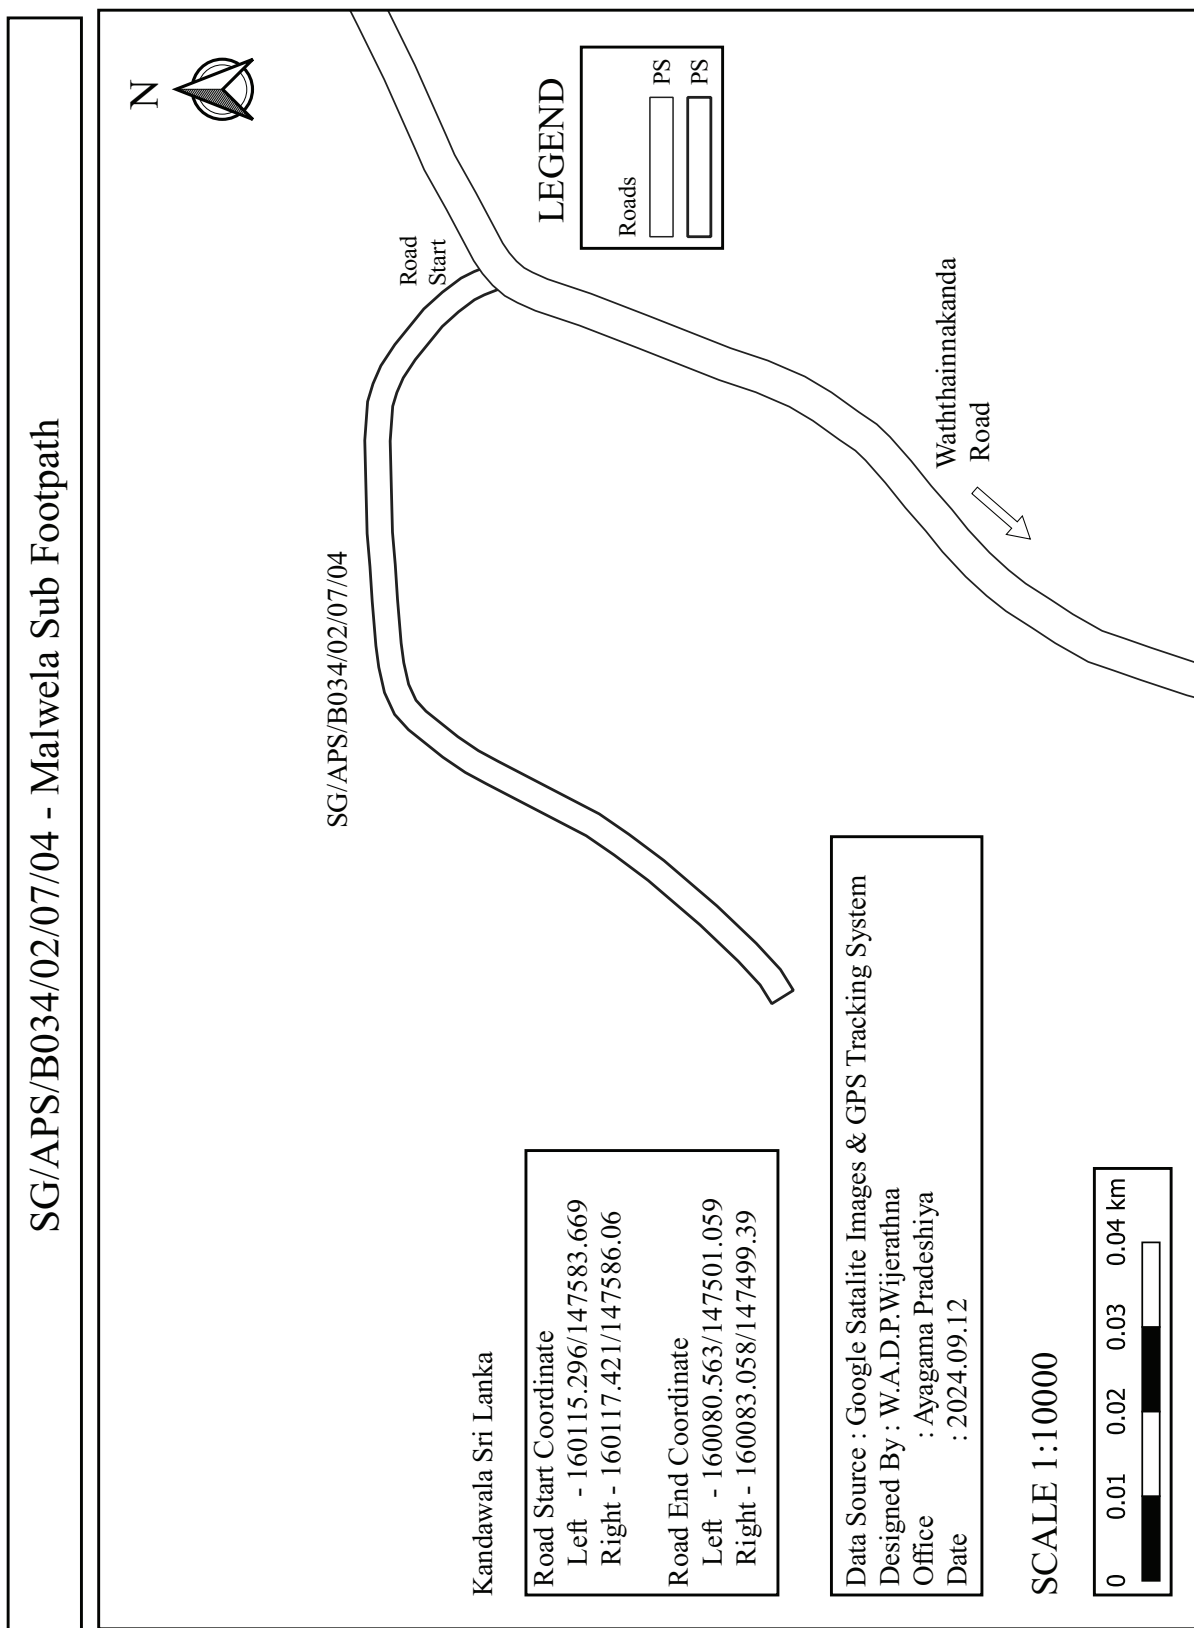


## SG/APS/B034/02/07/05 - Waththainnakanda Kekunagahahena Road

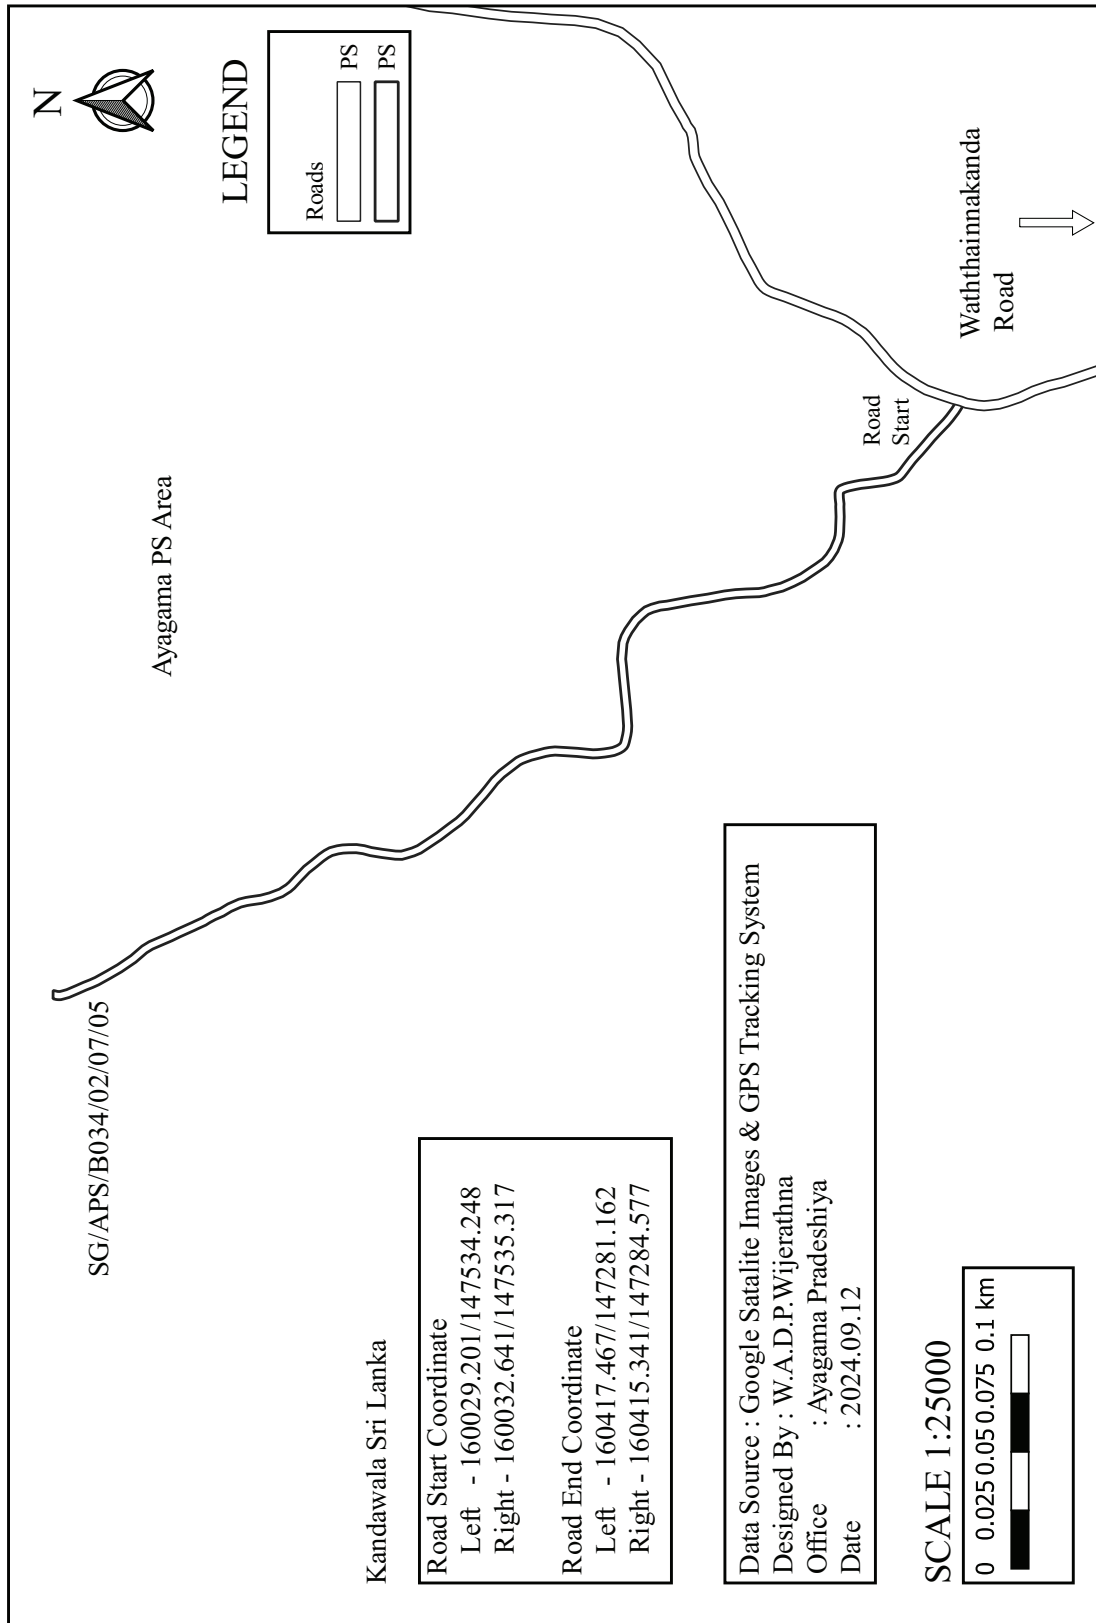


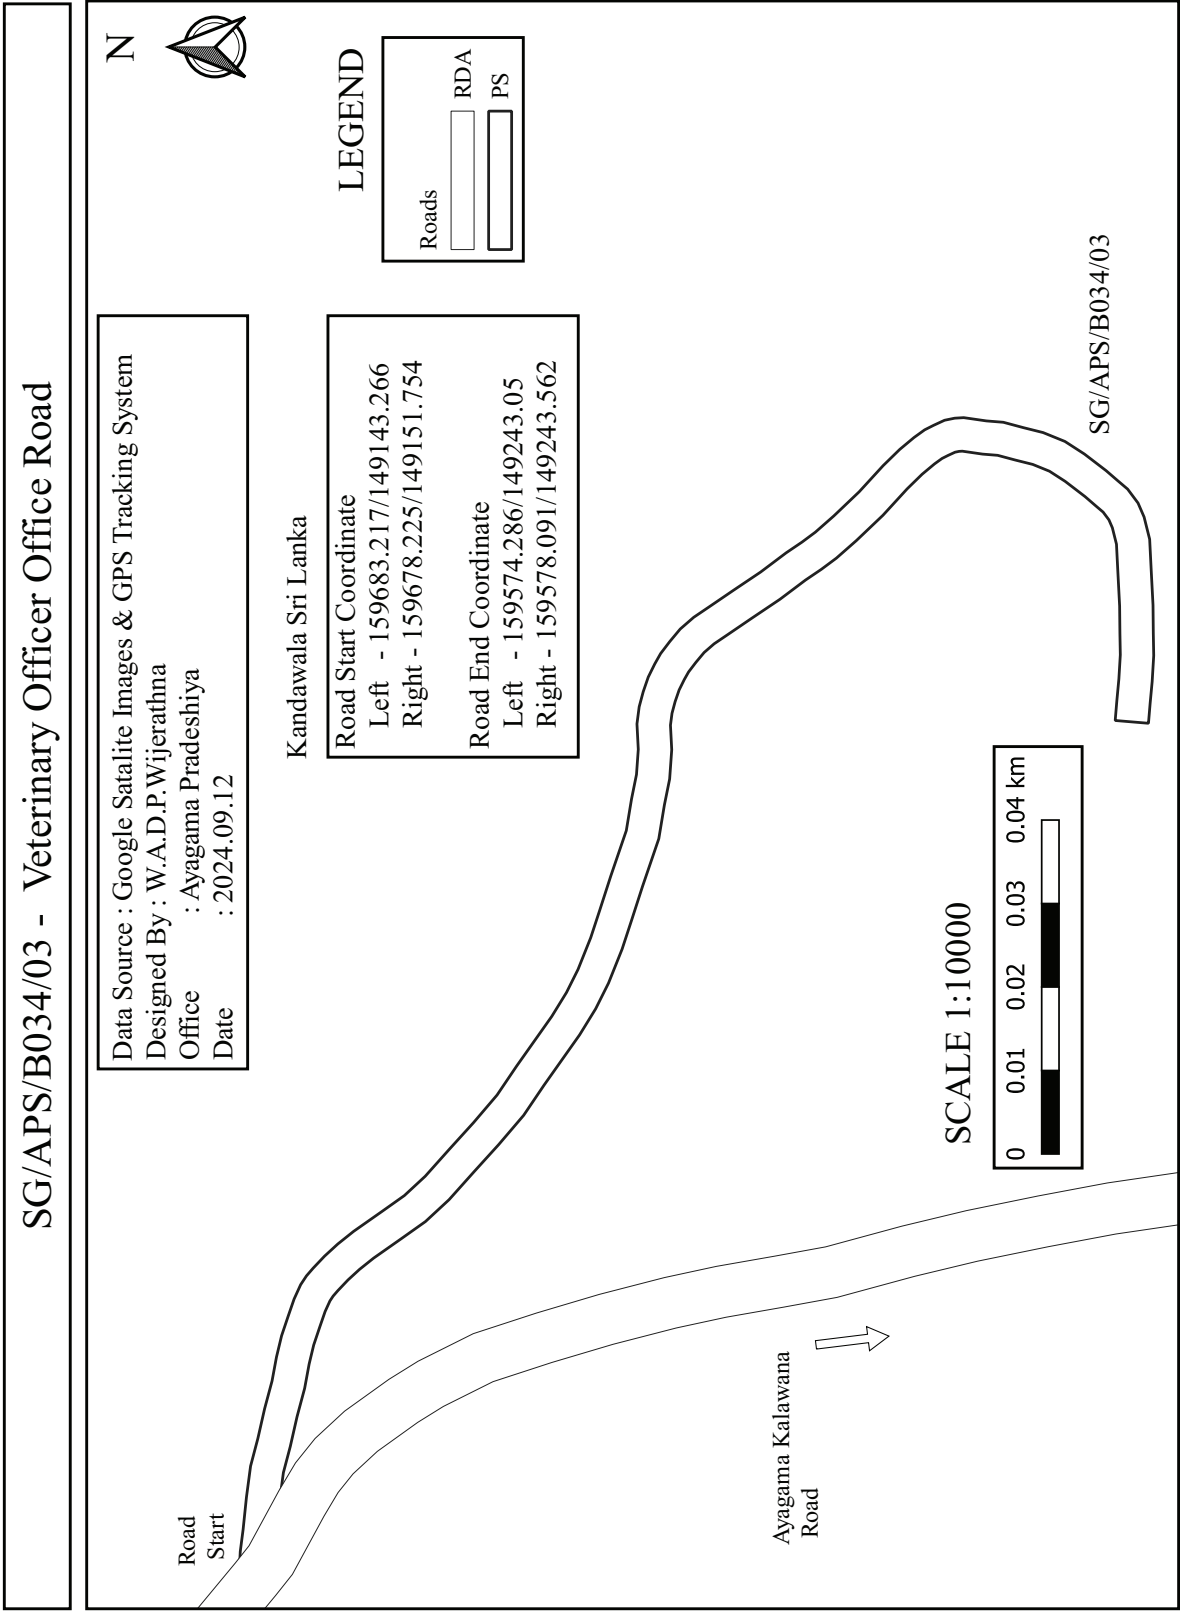


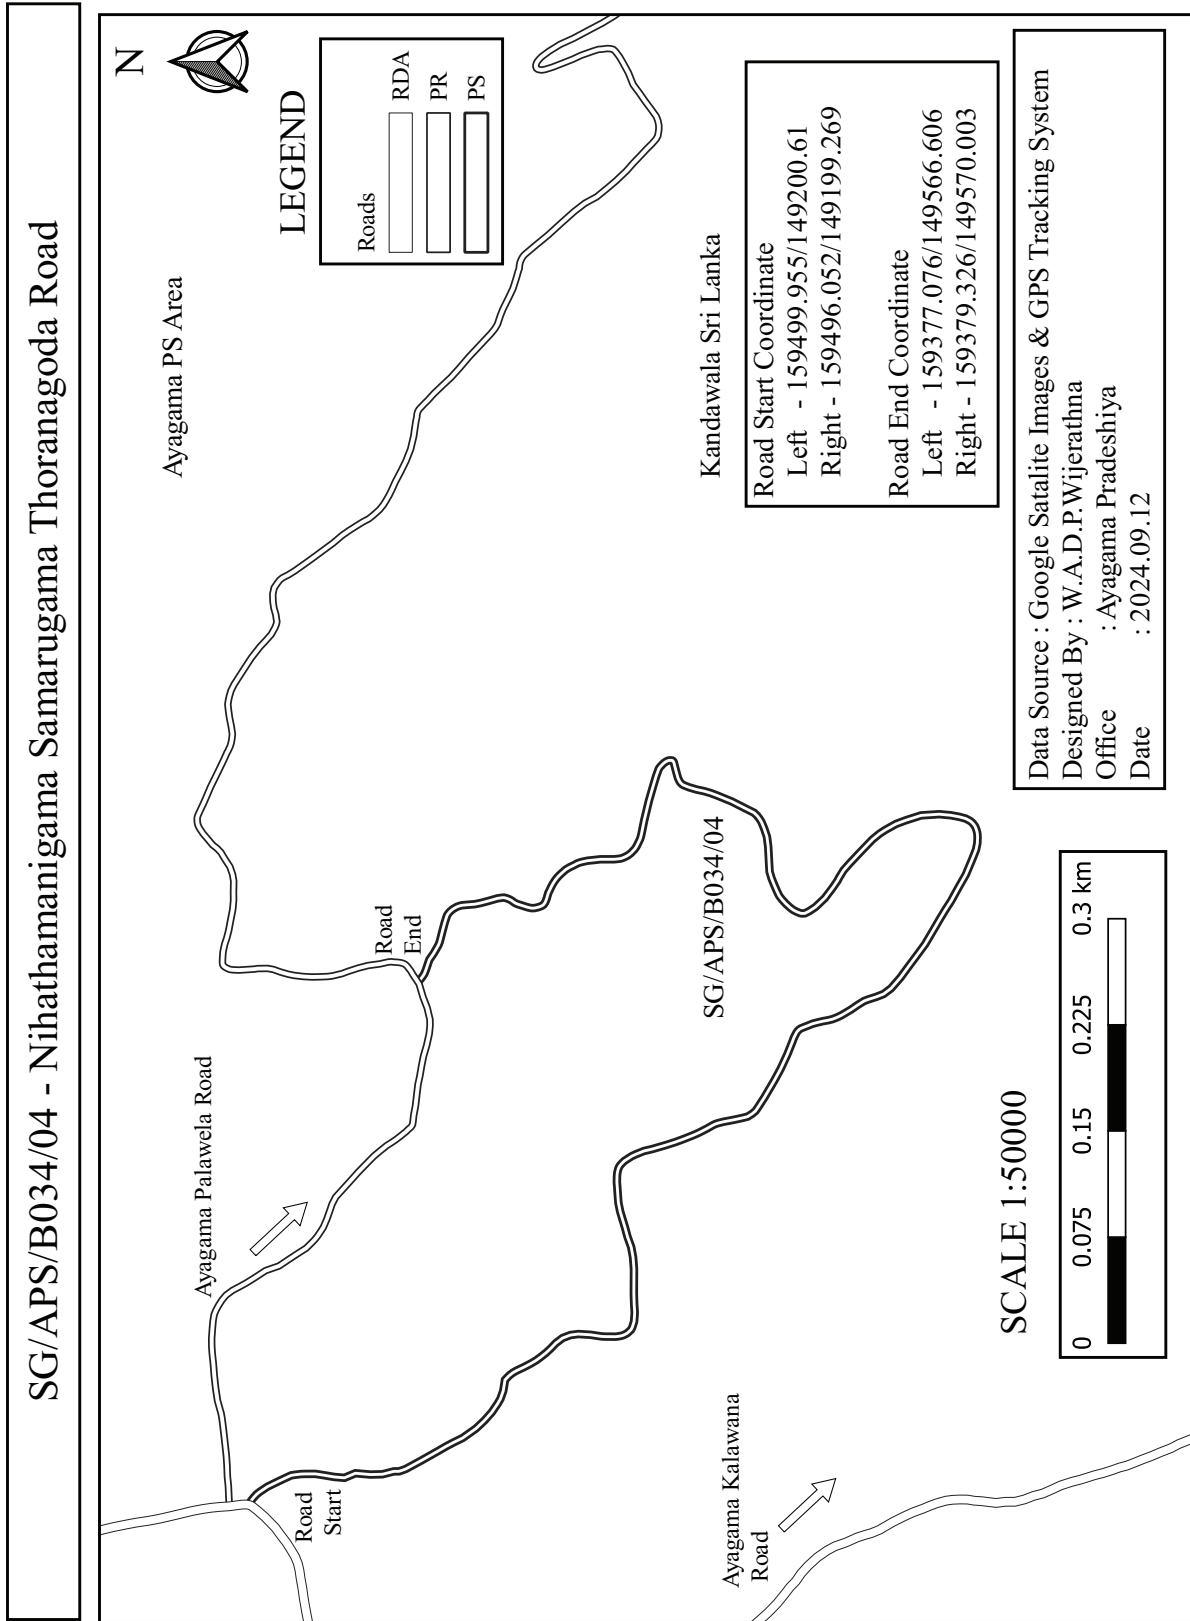


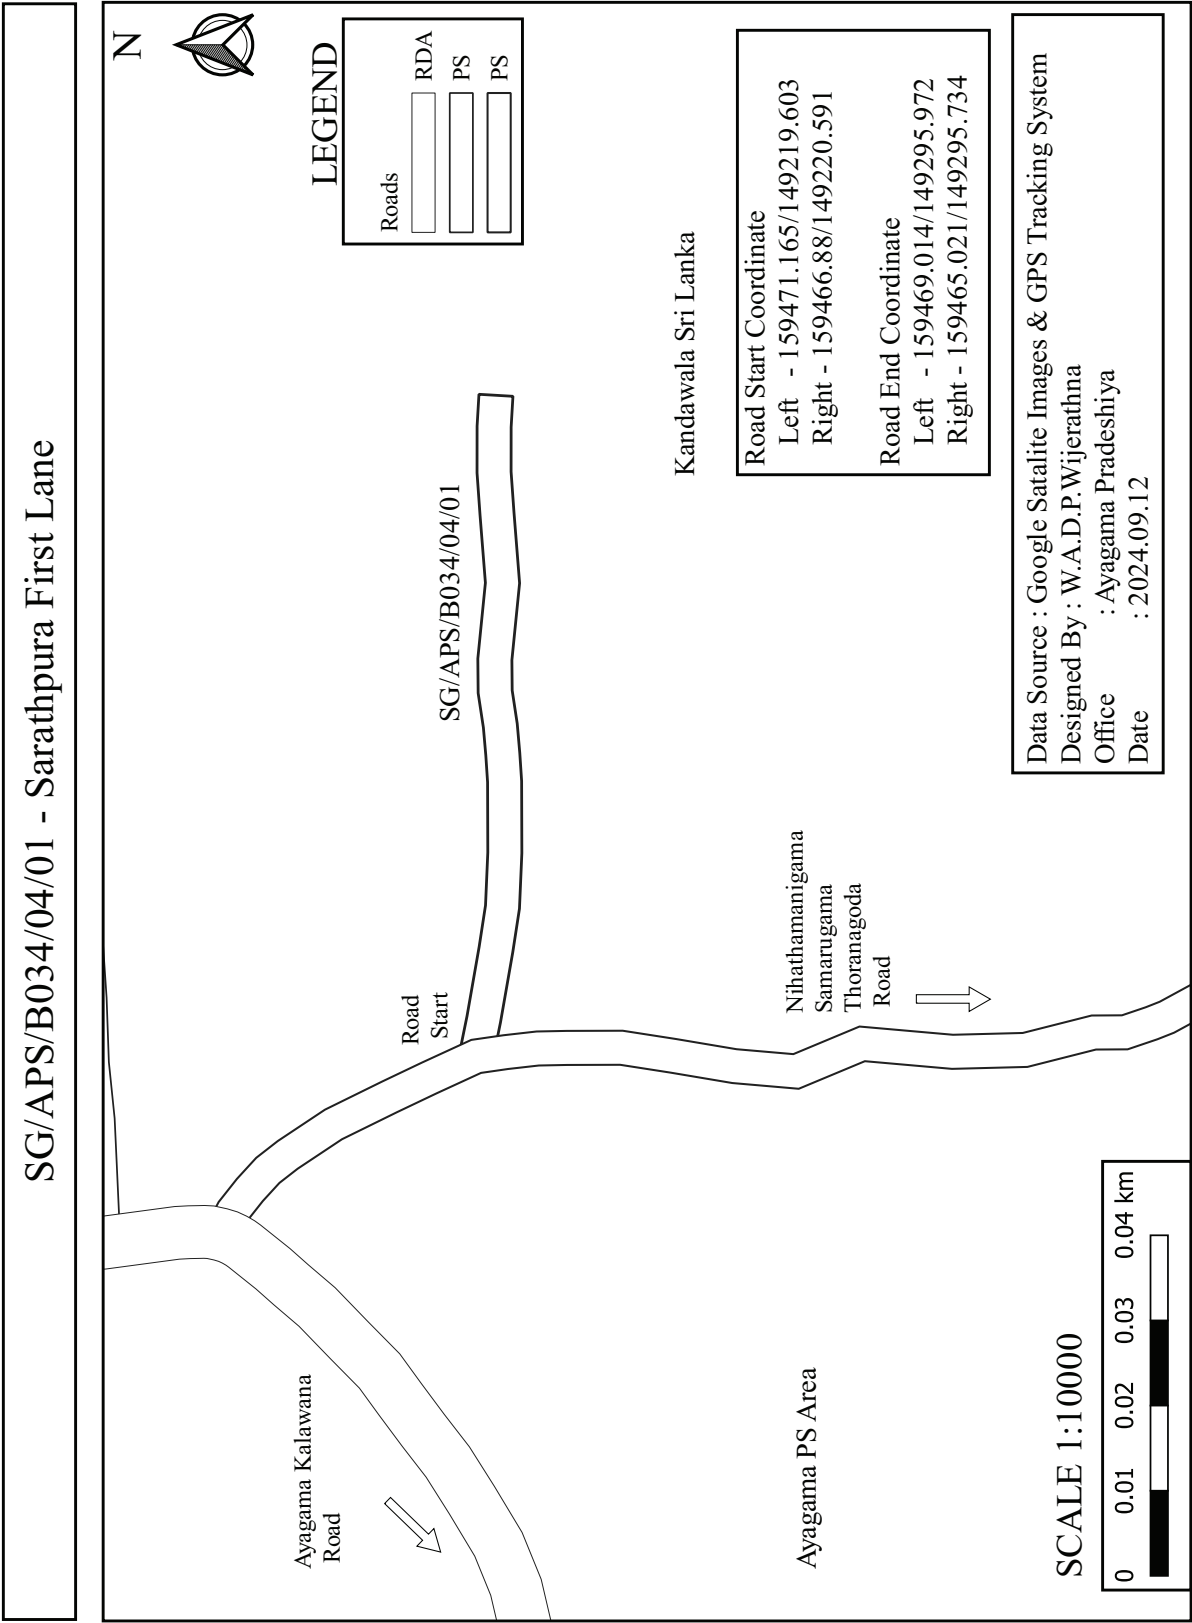





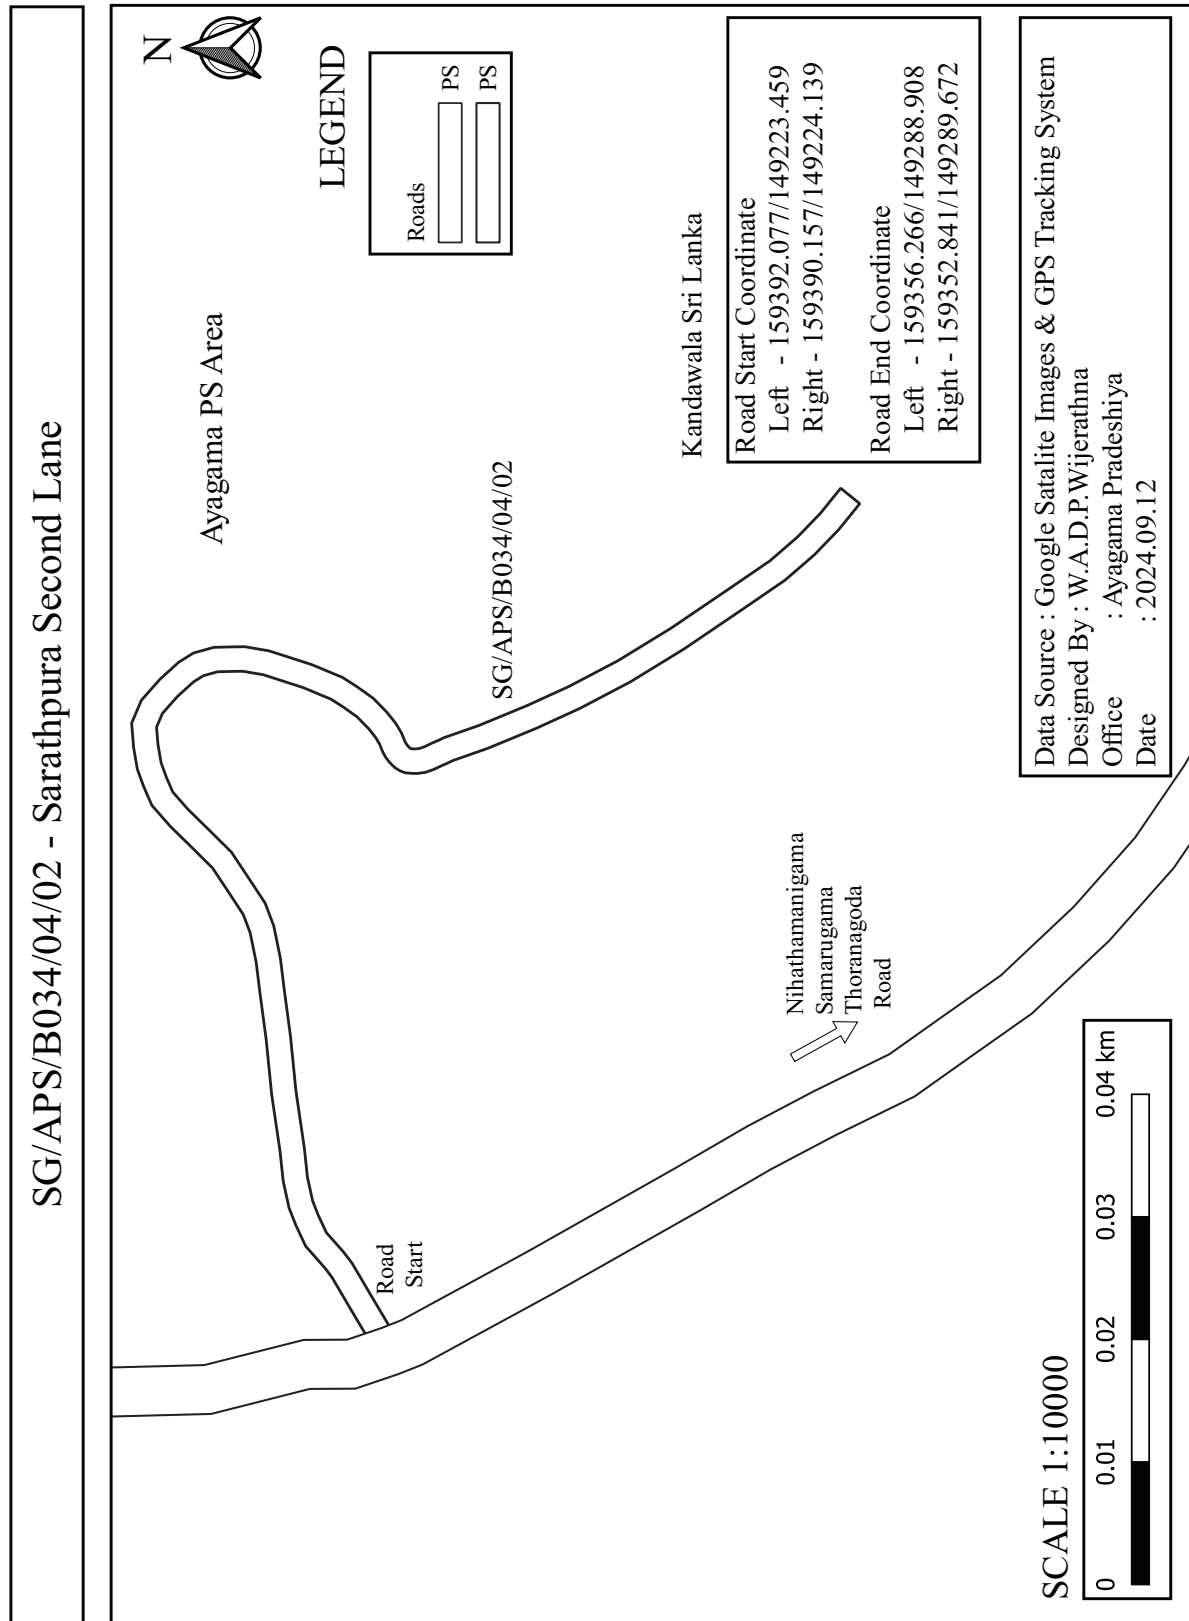


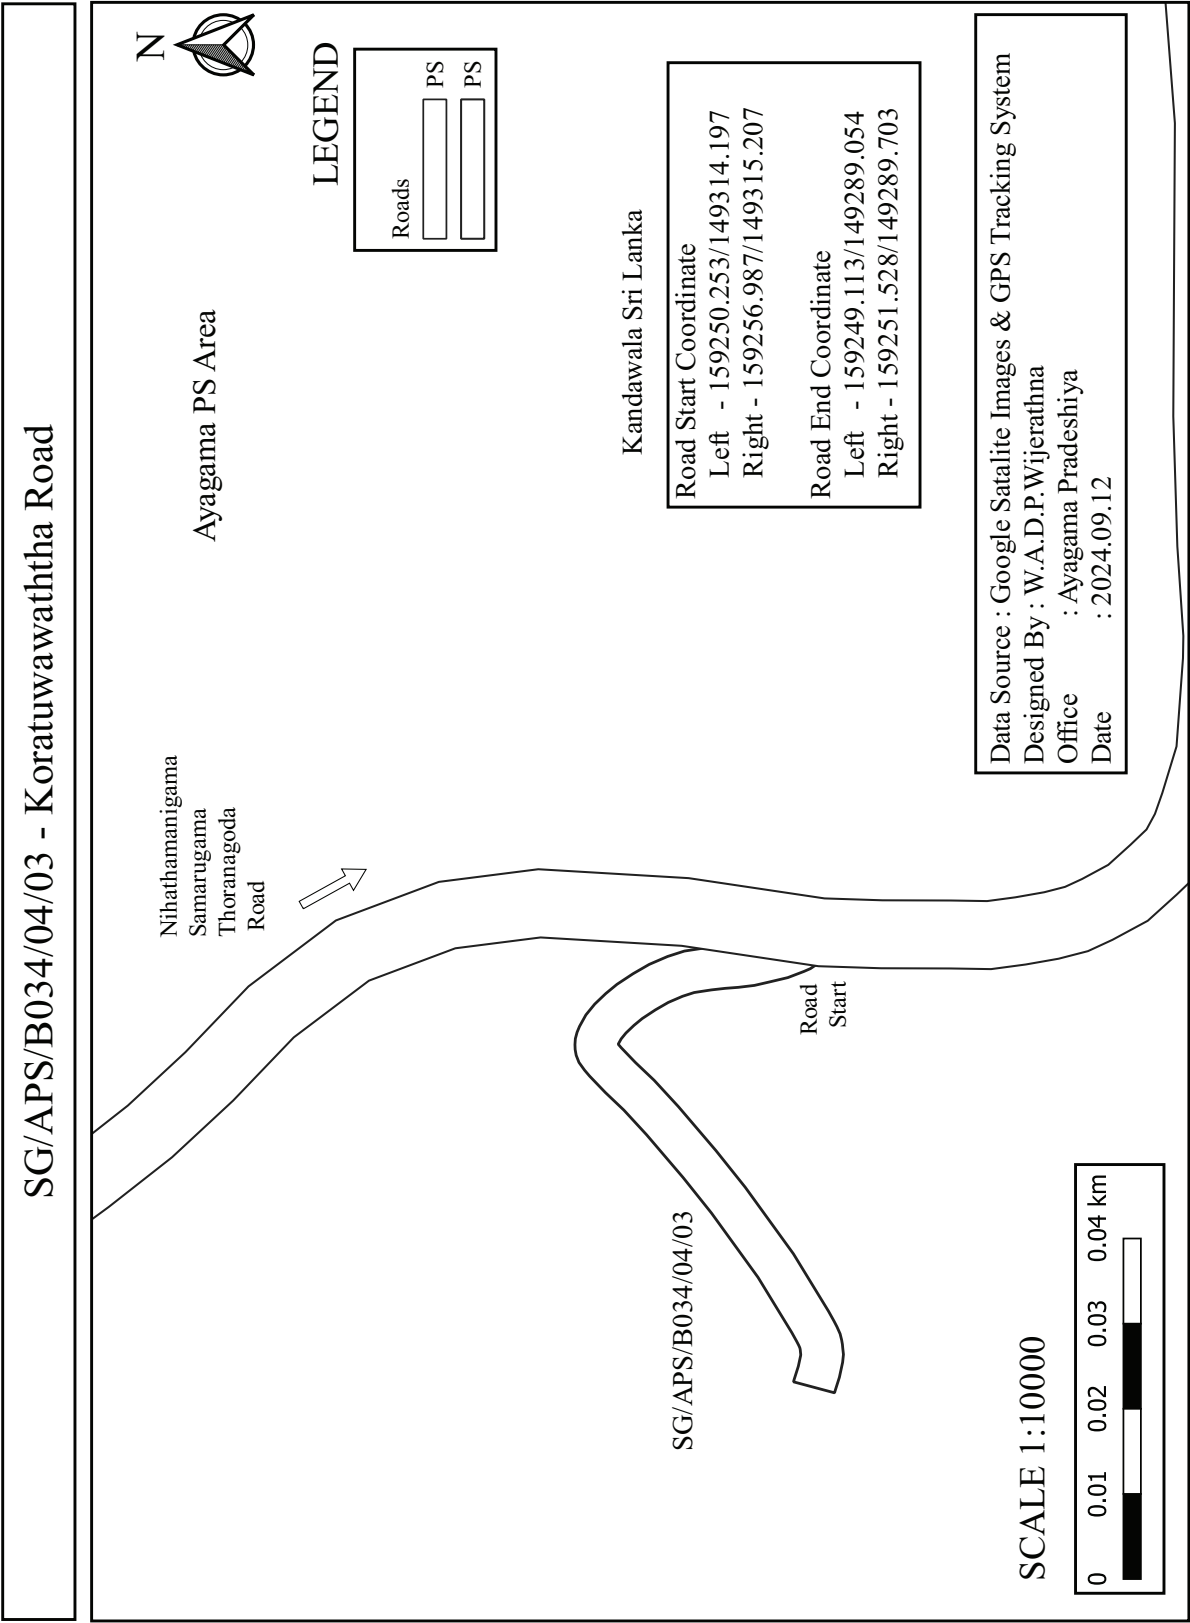


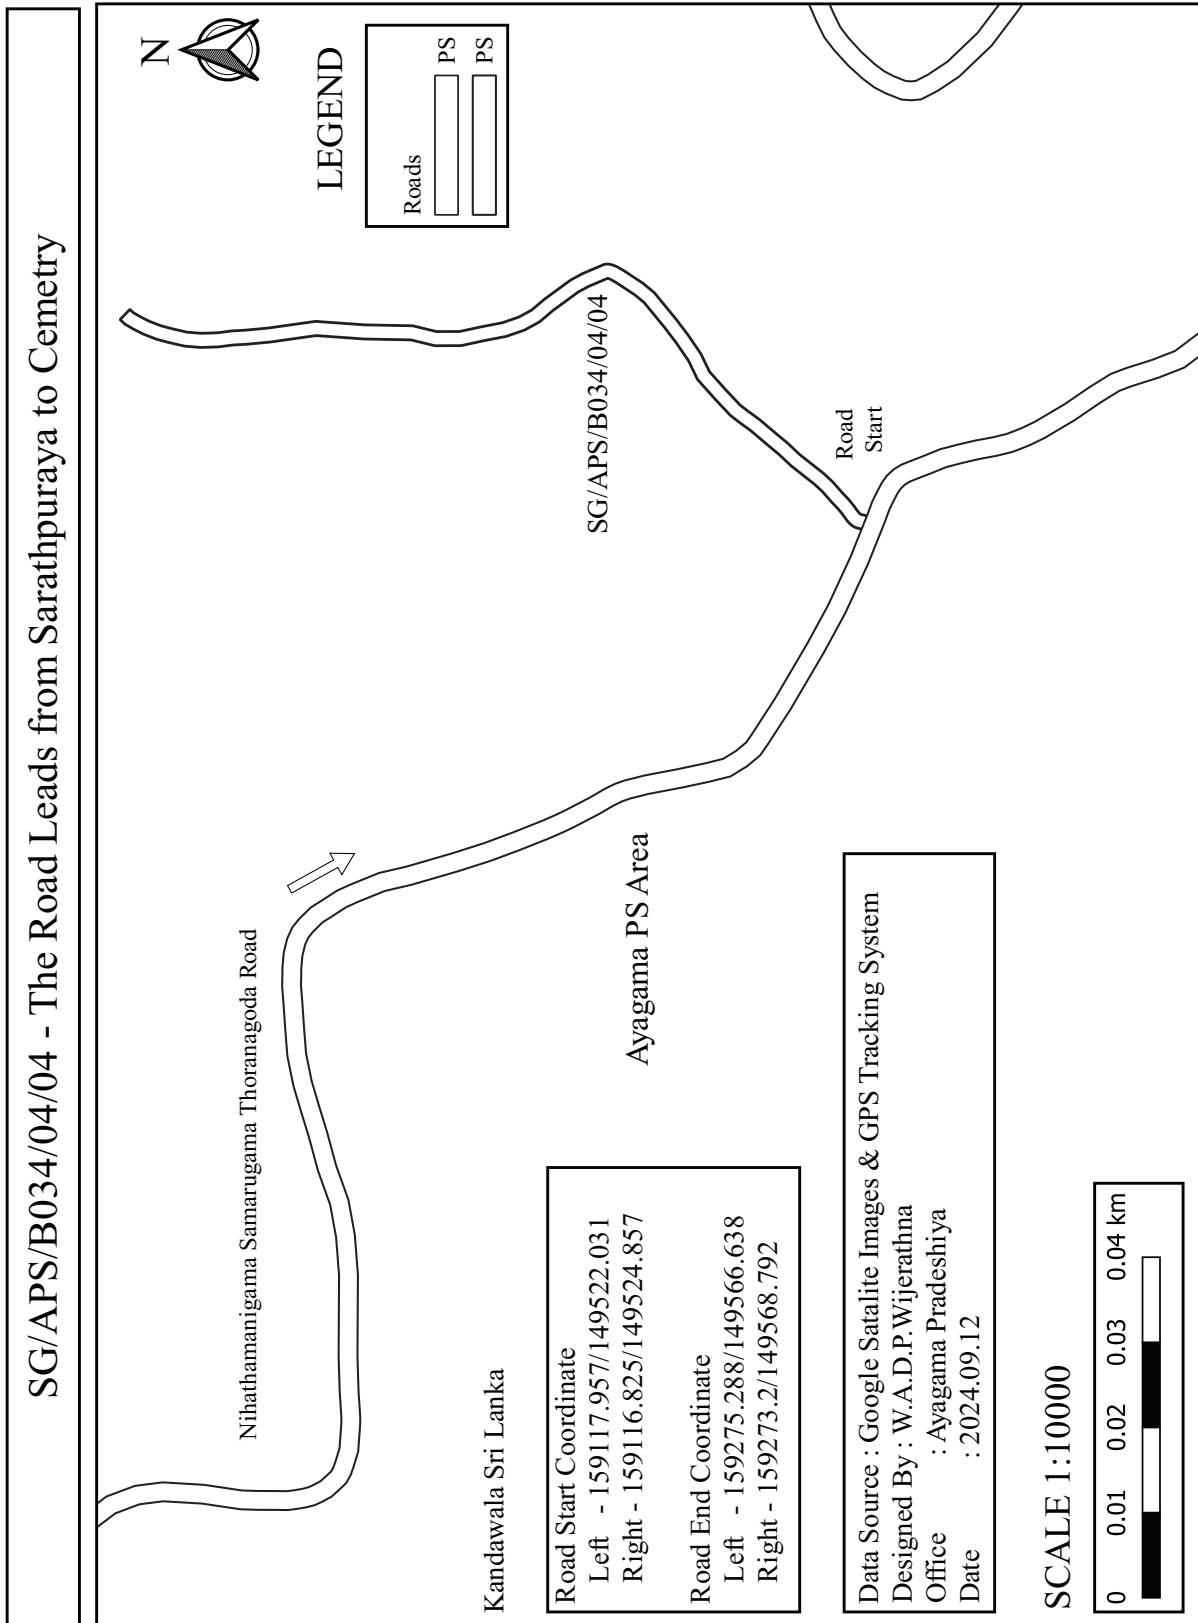


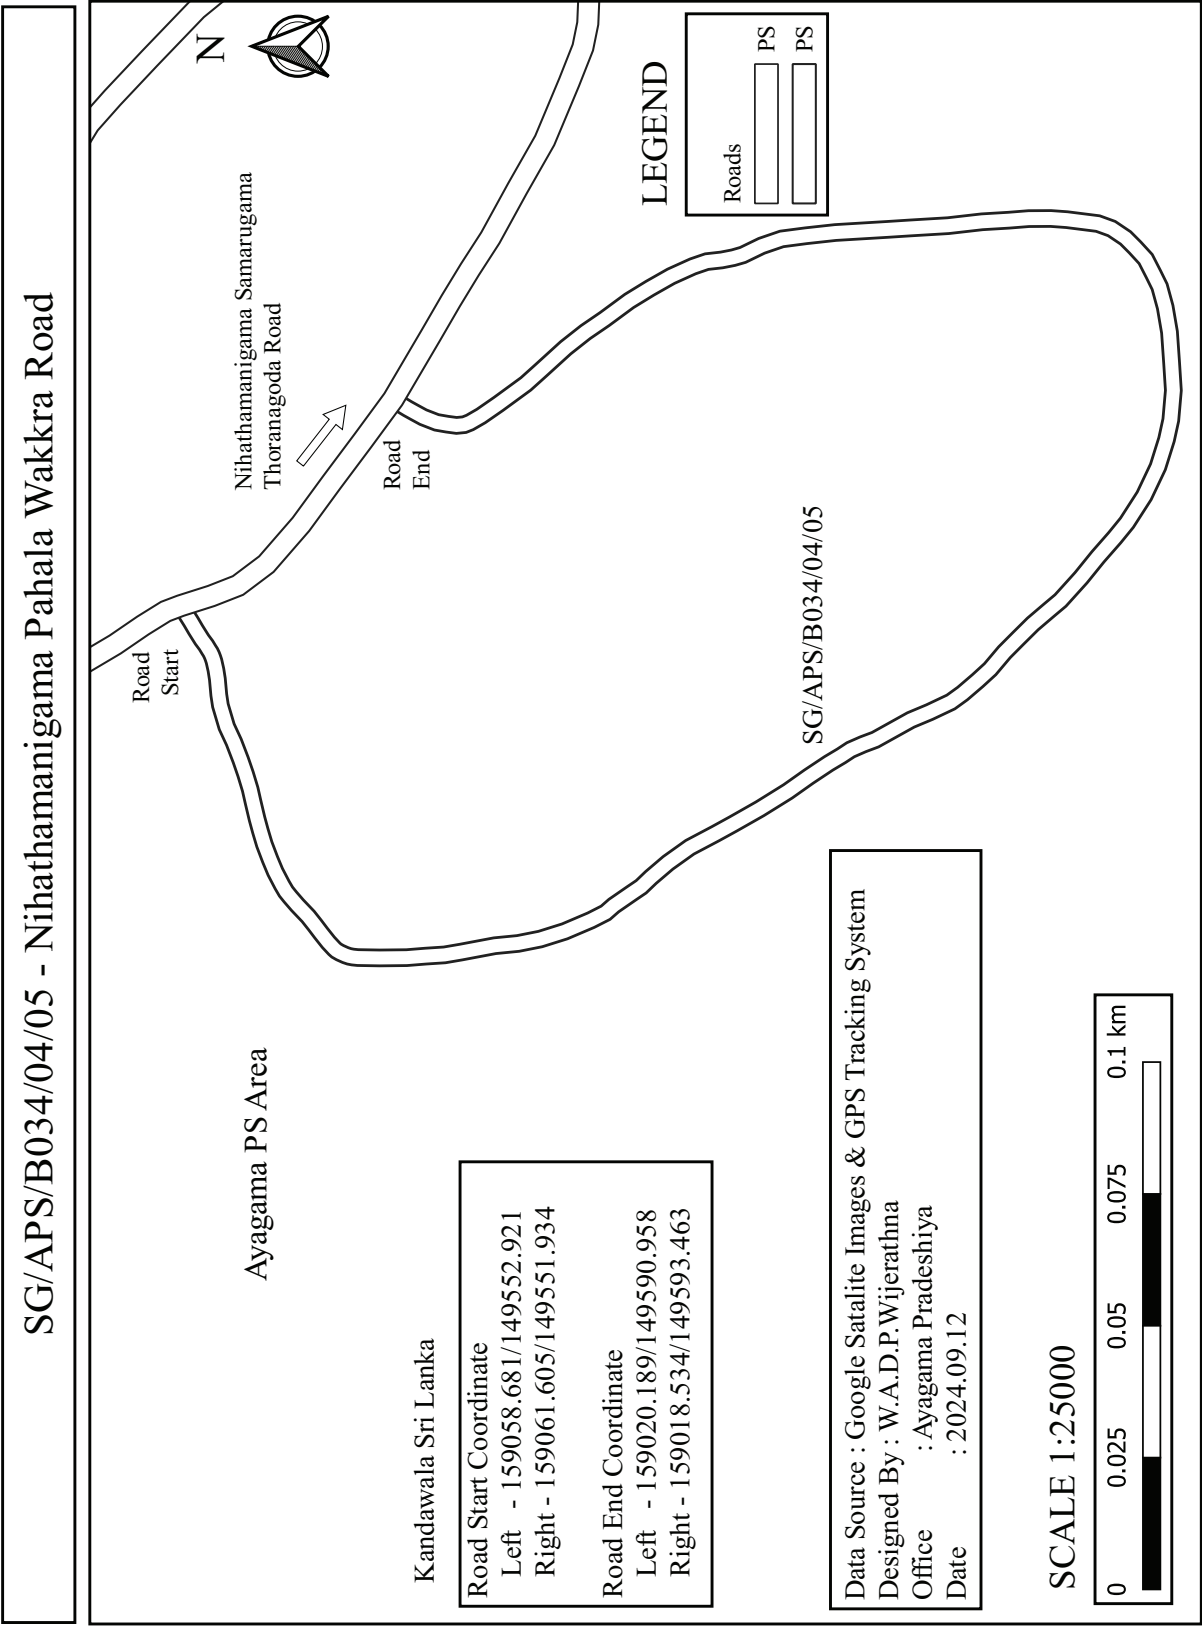

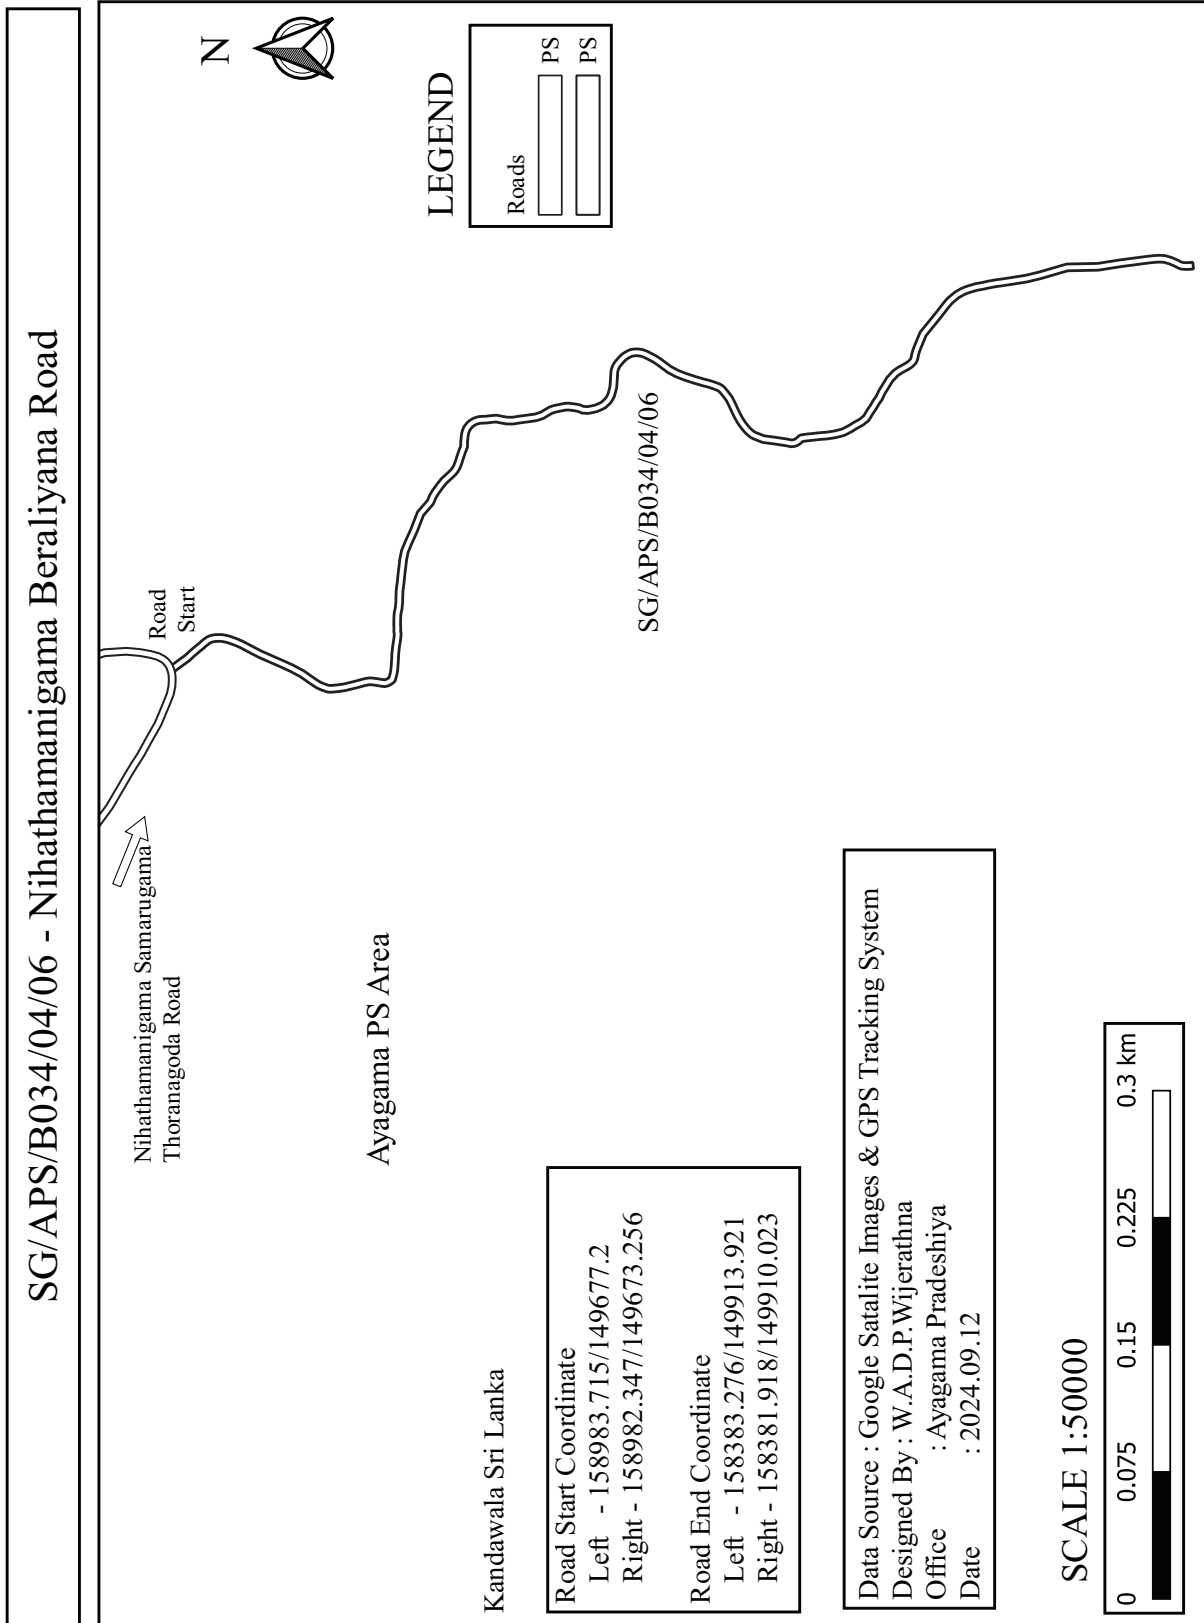


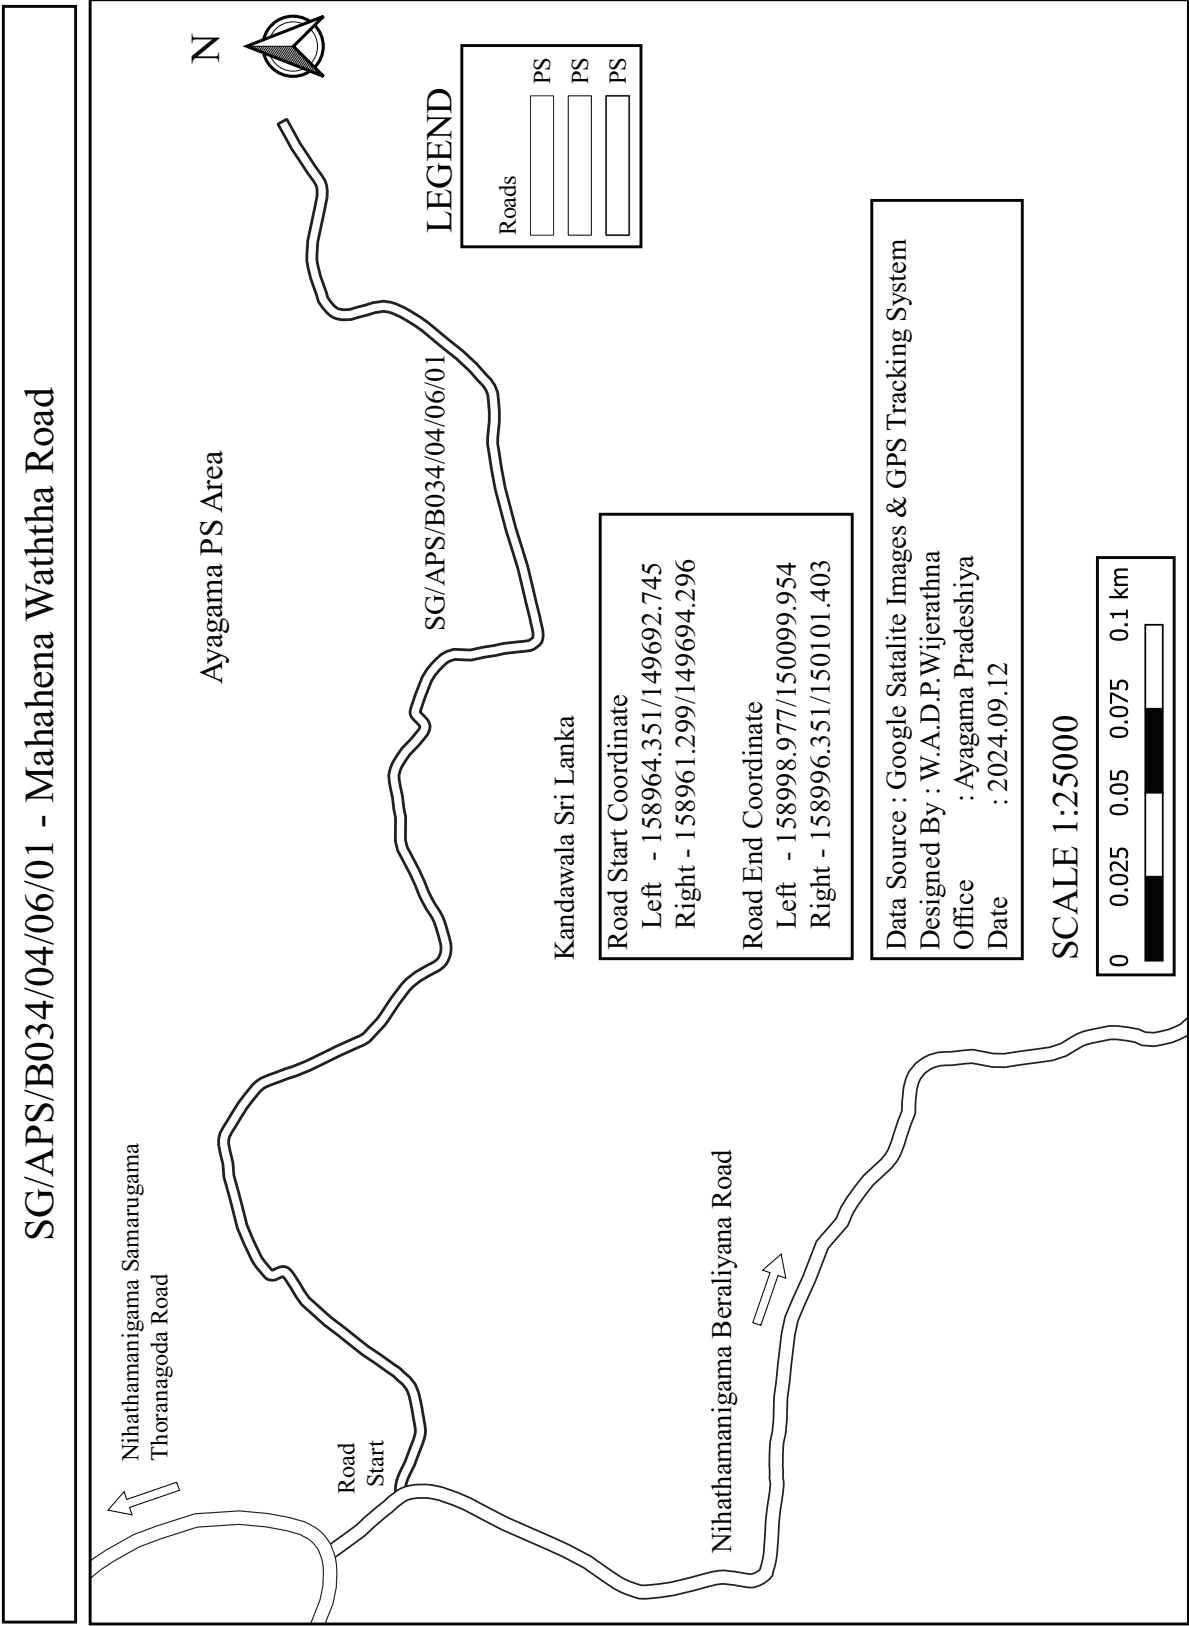


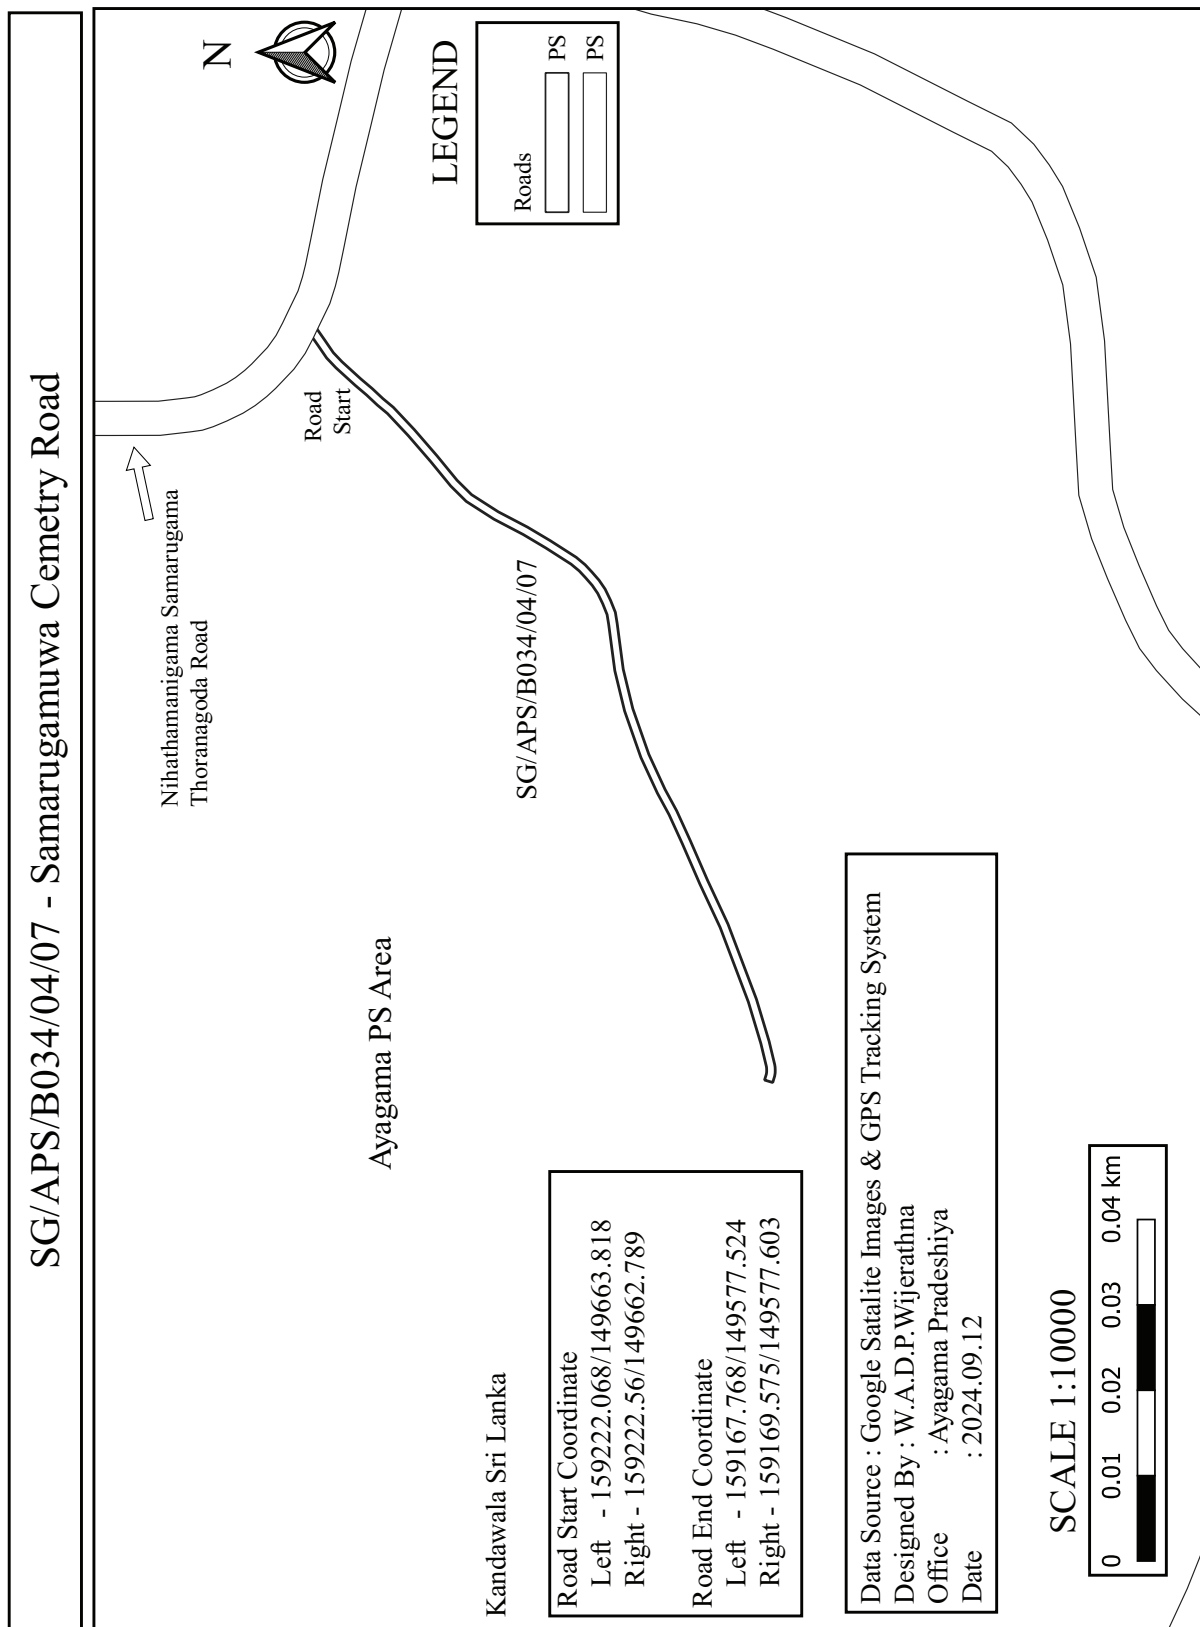


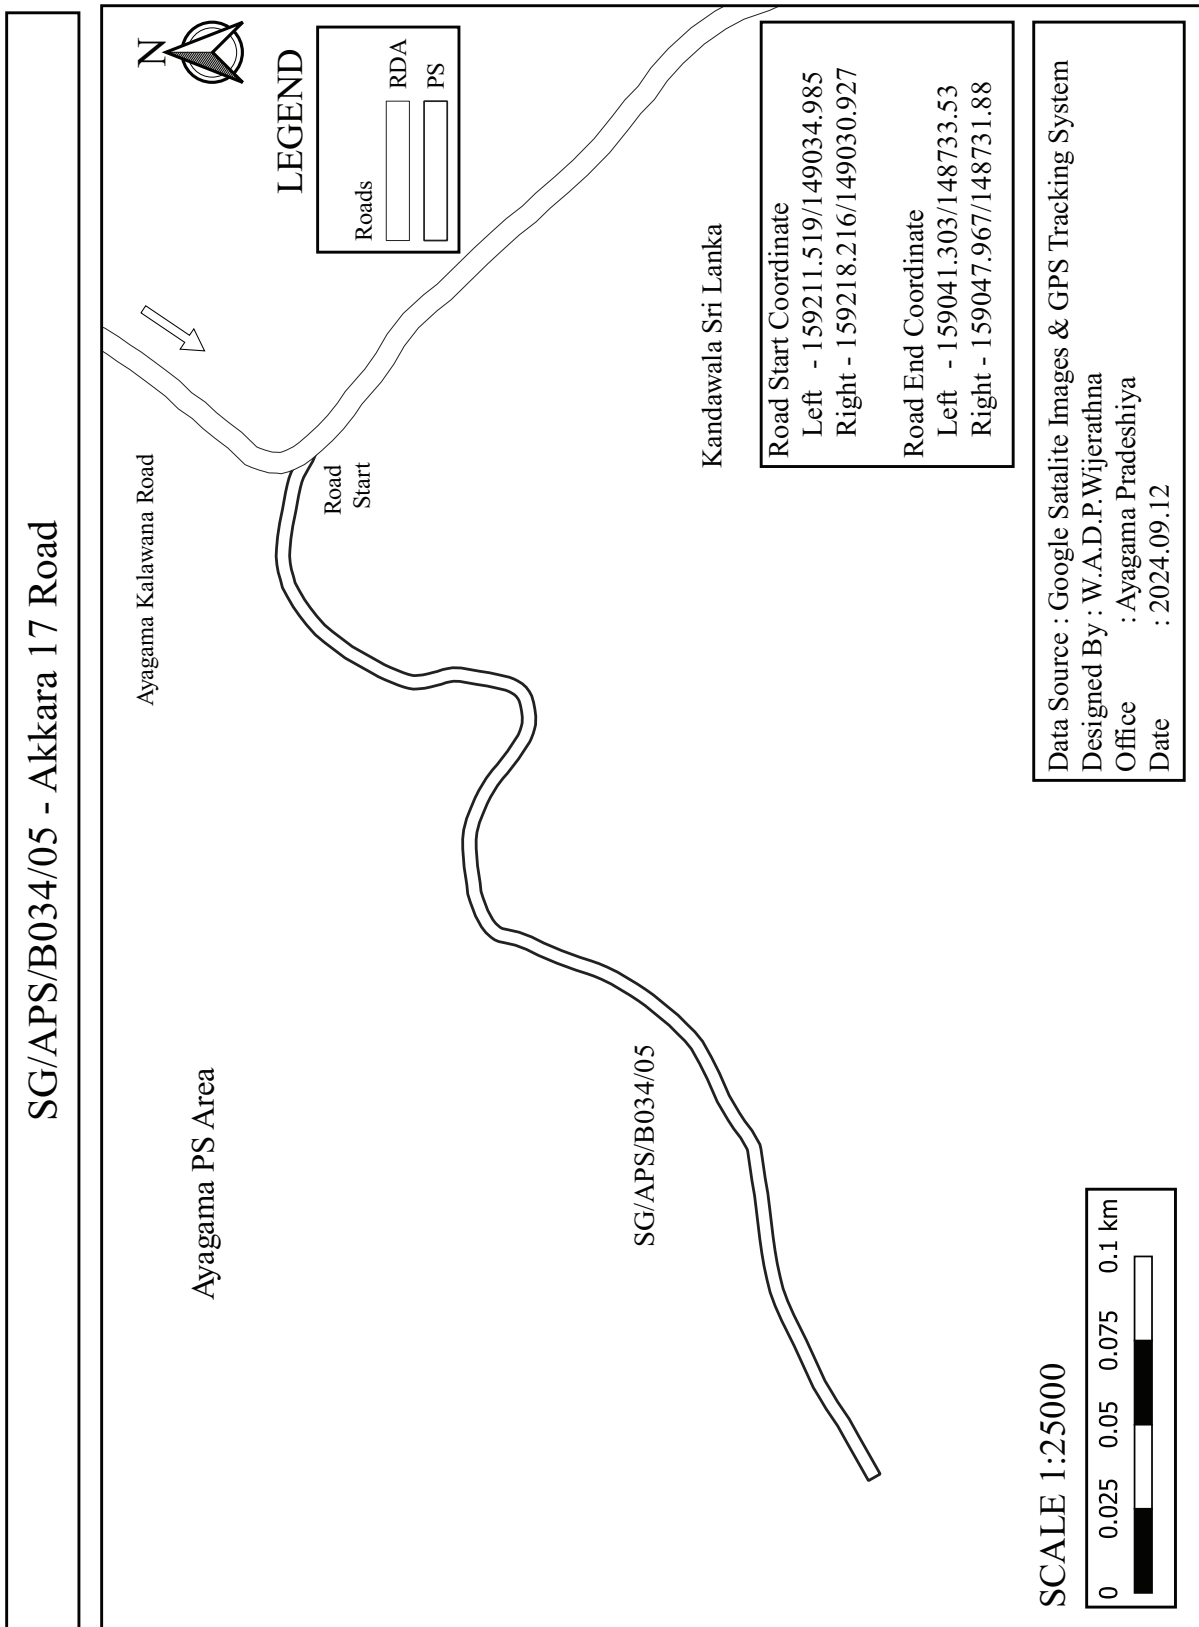





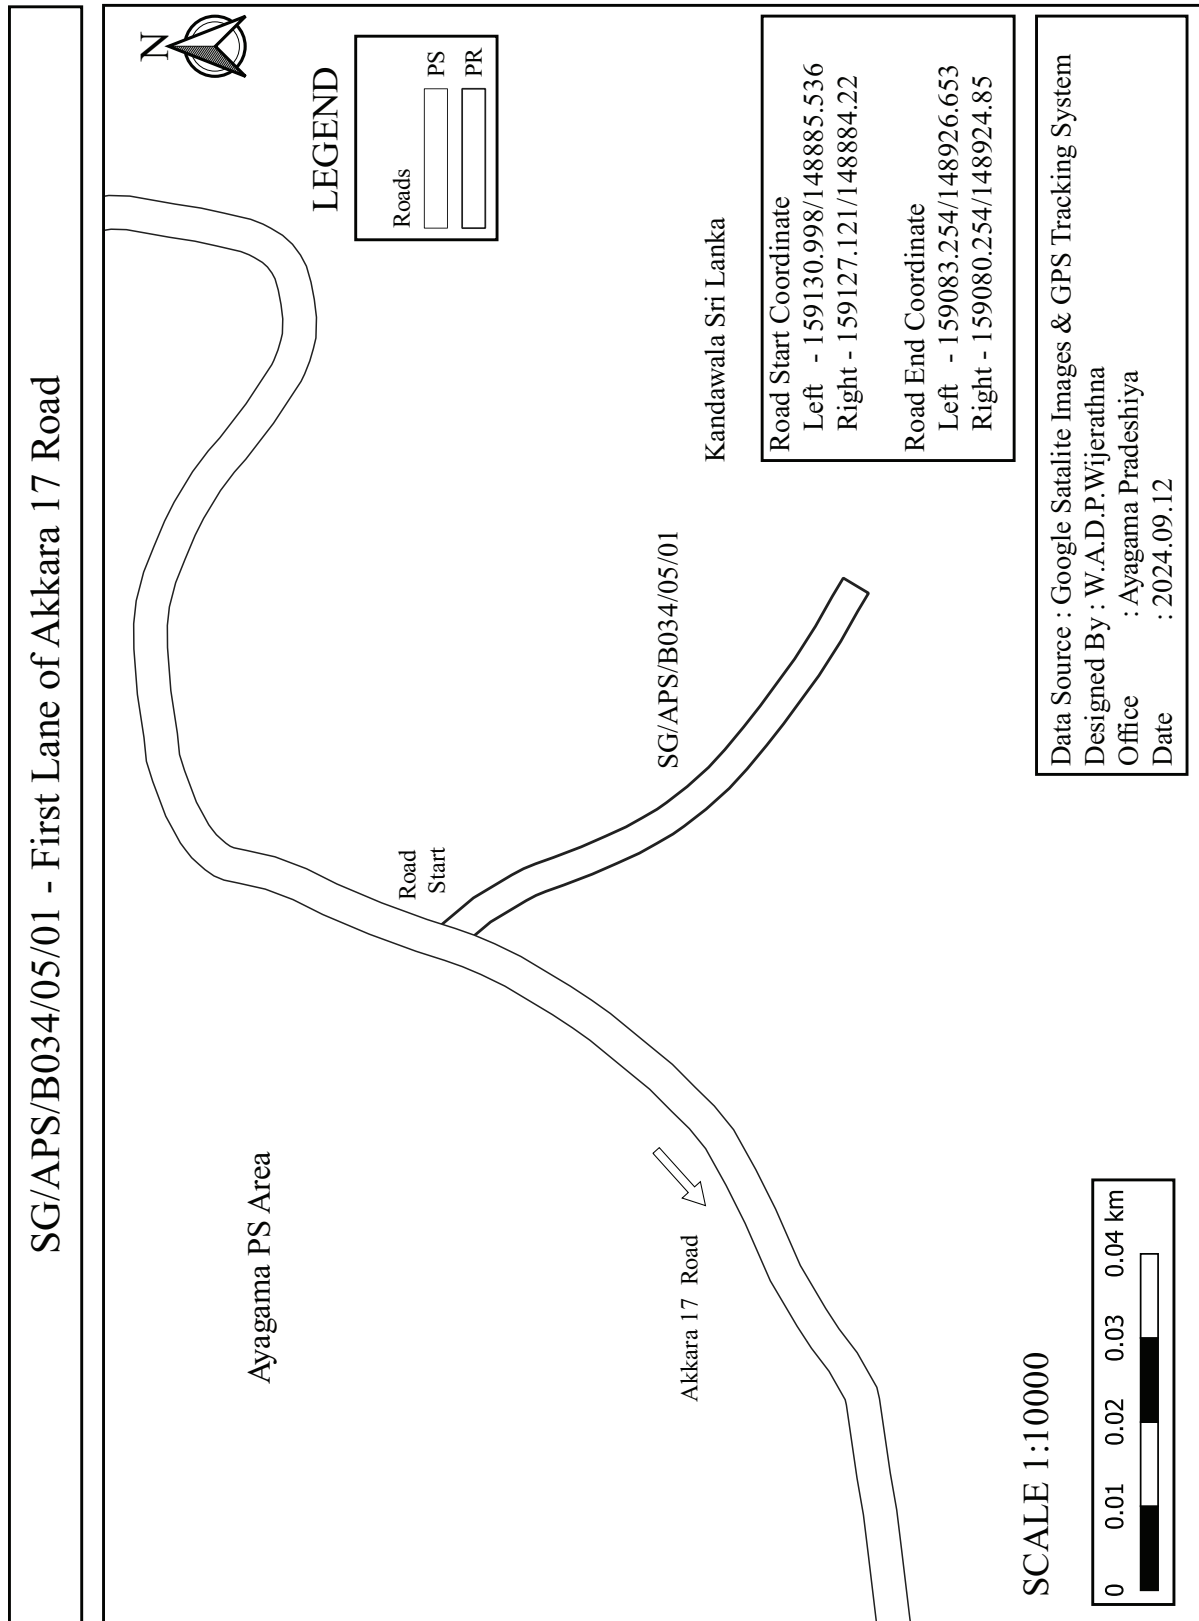


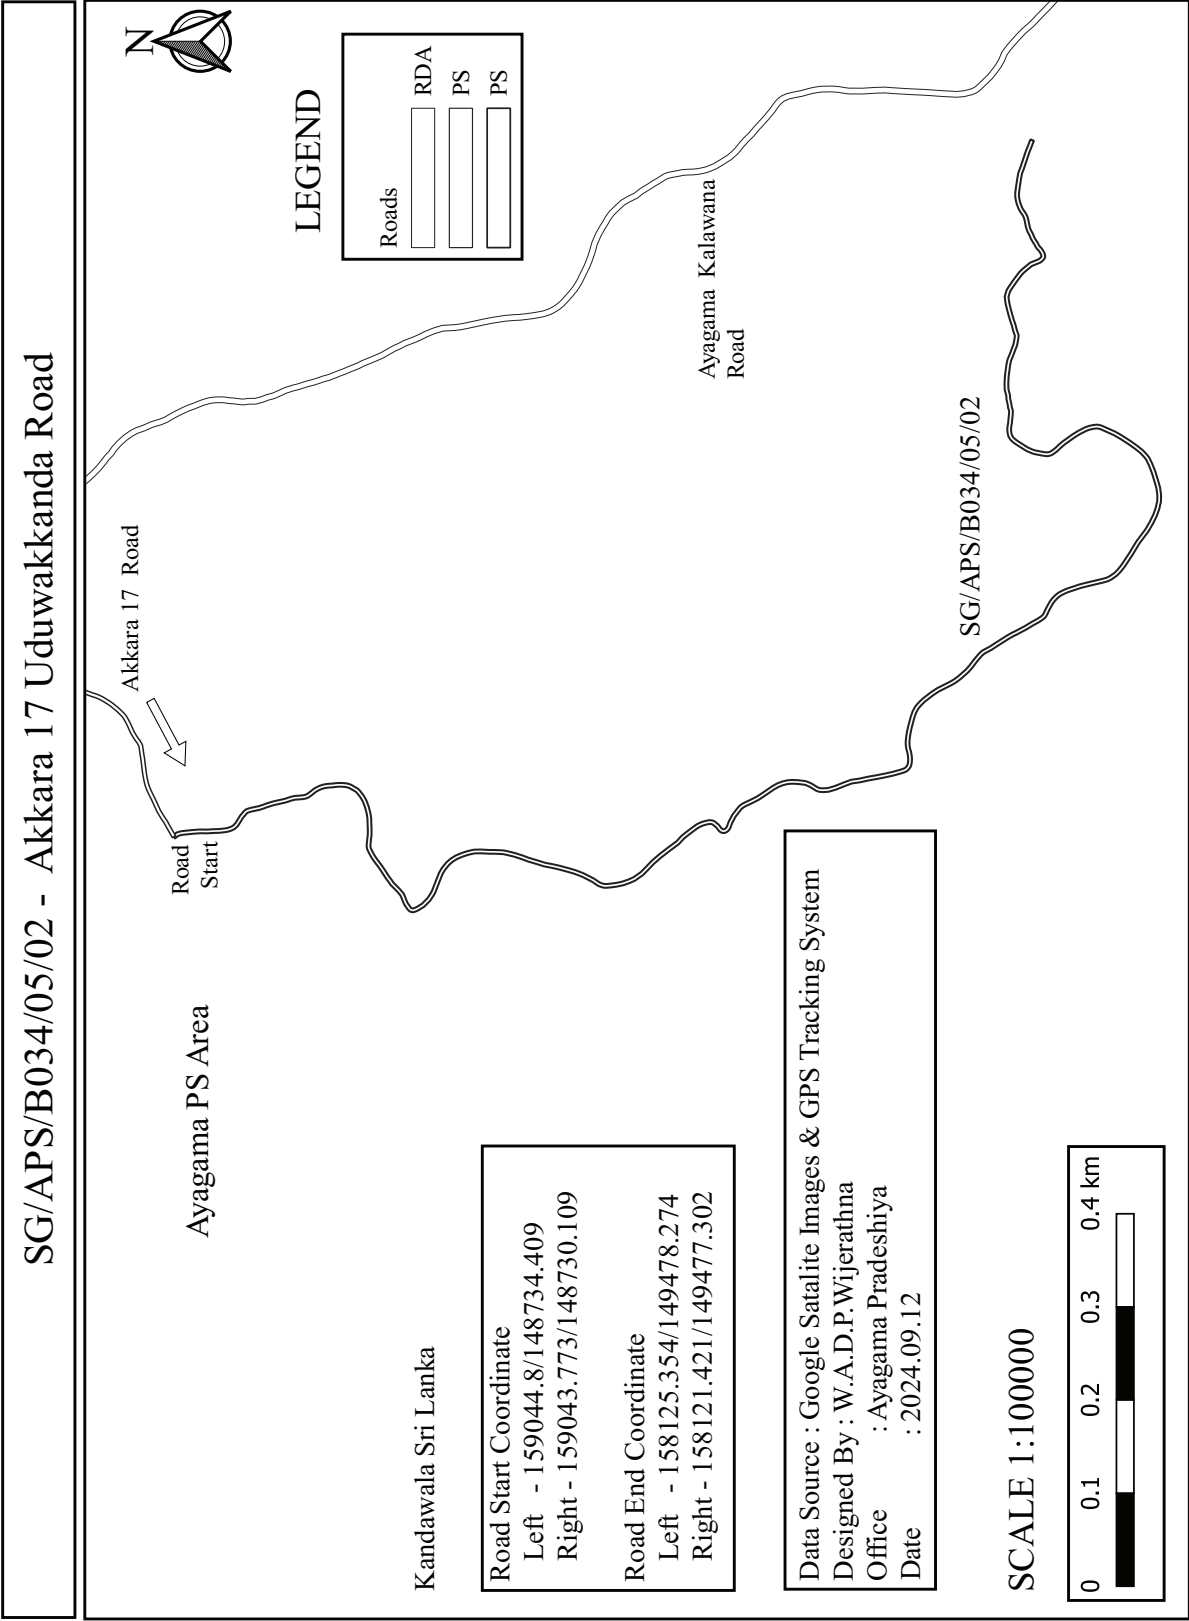


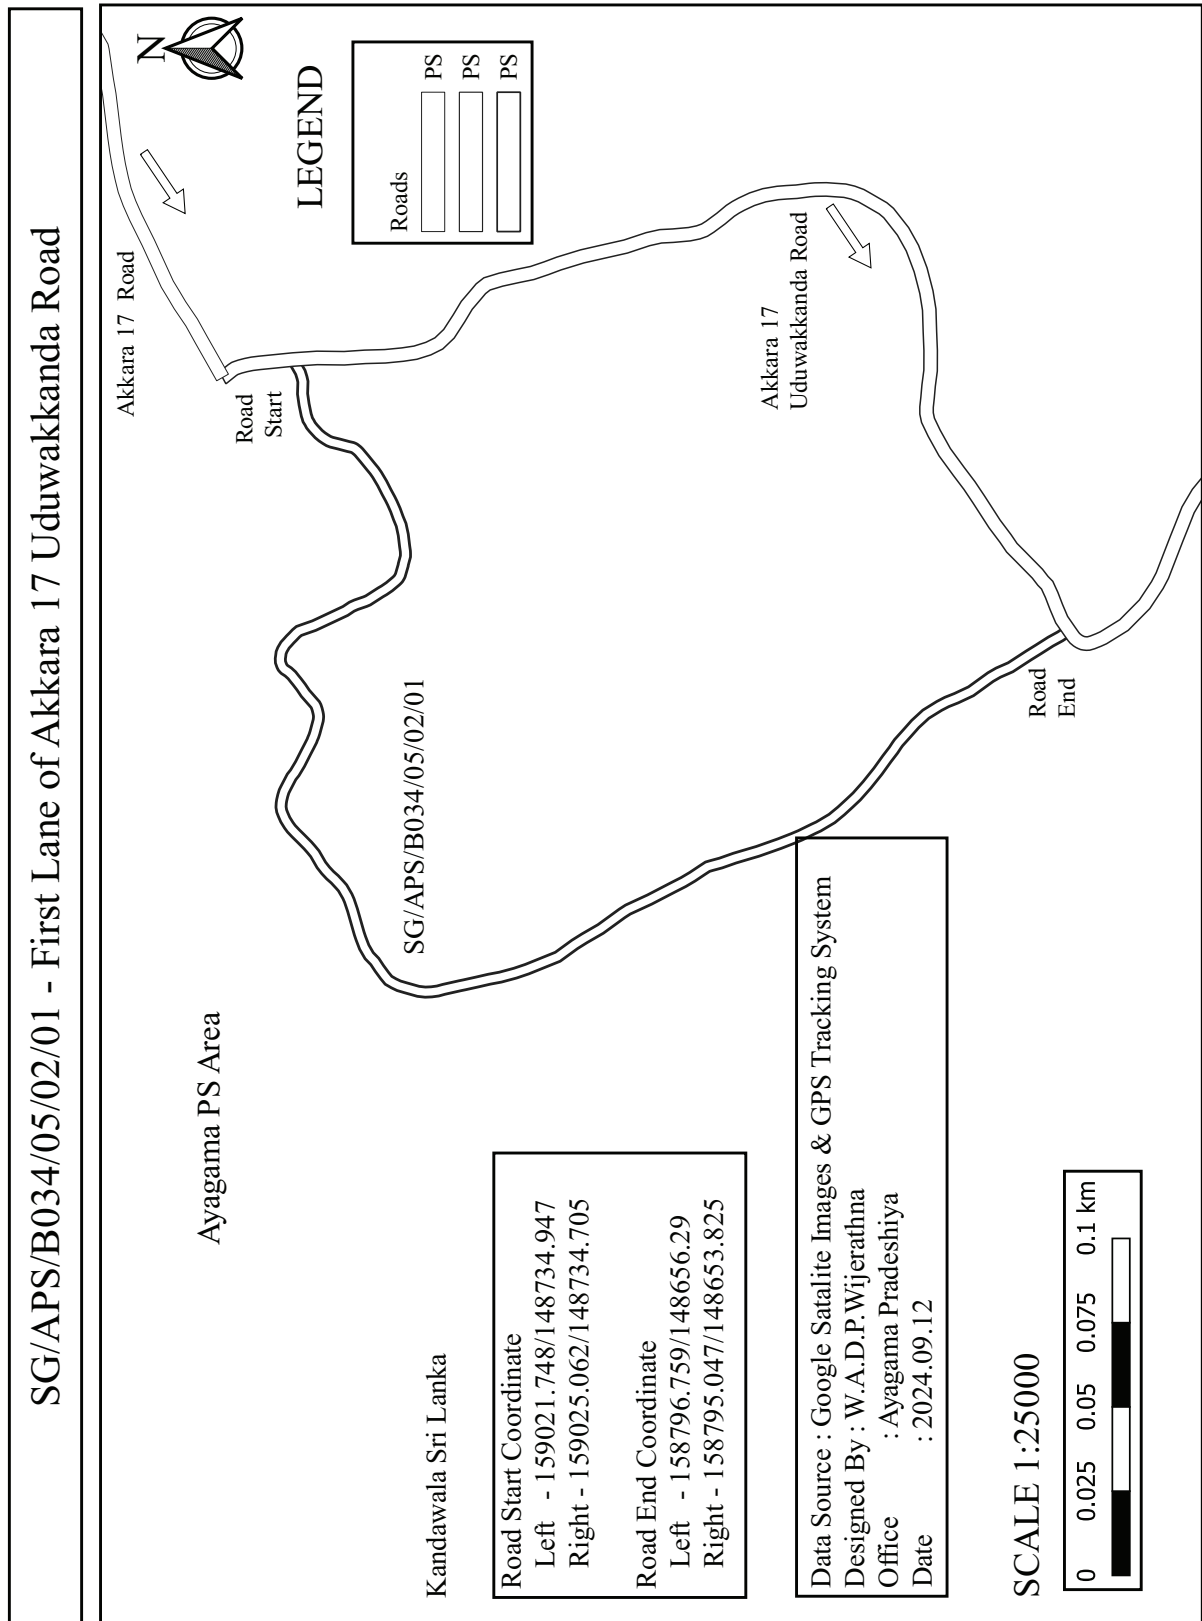

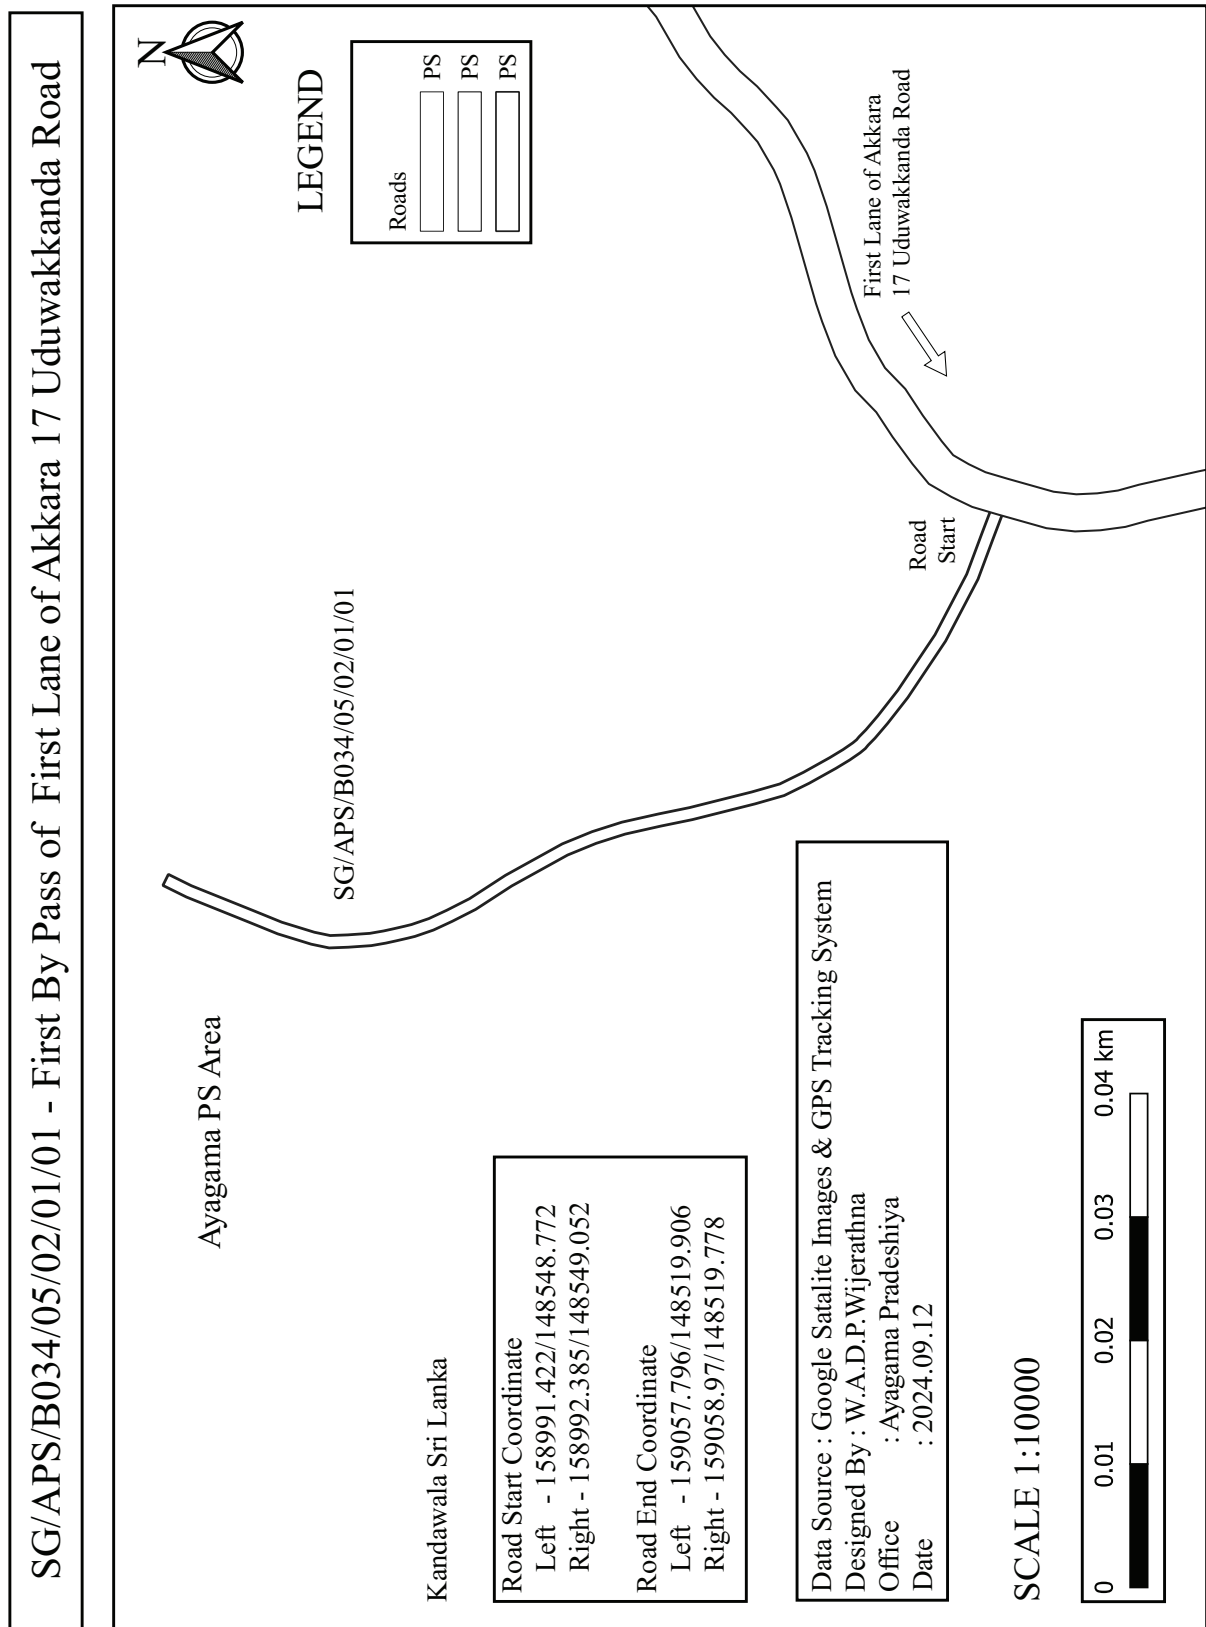

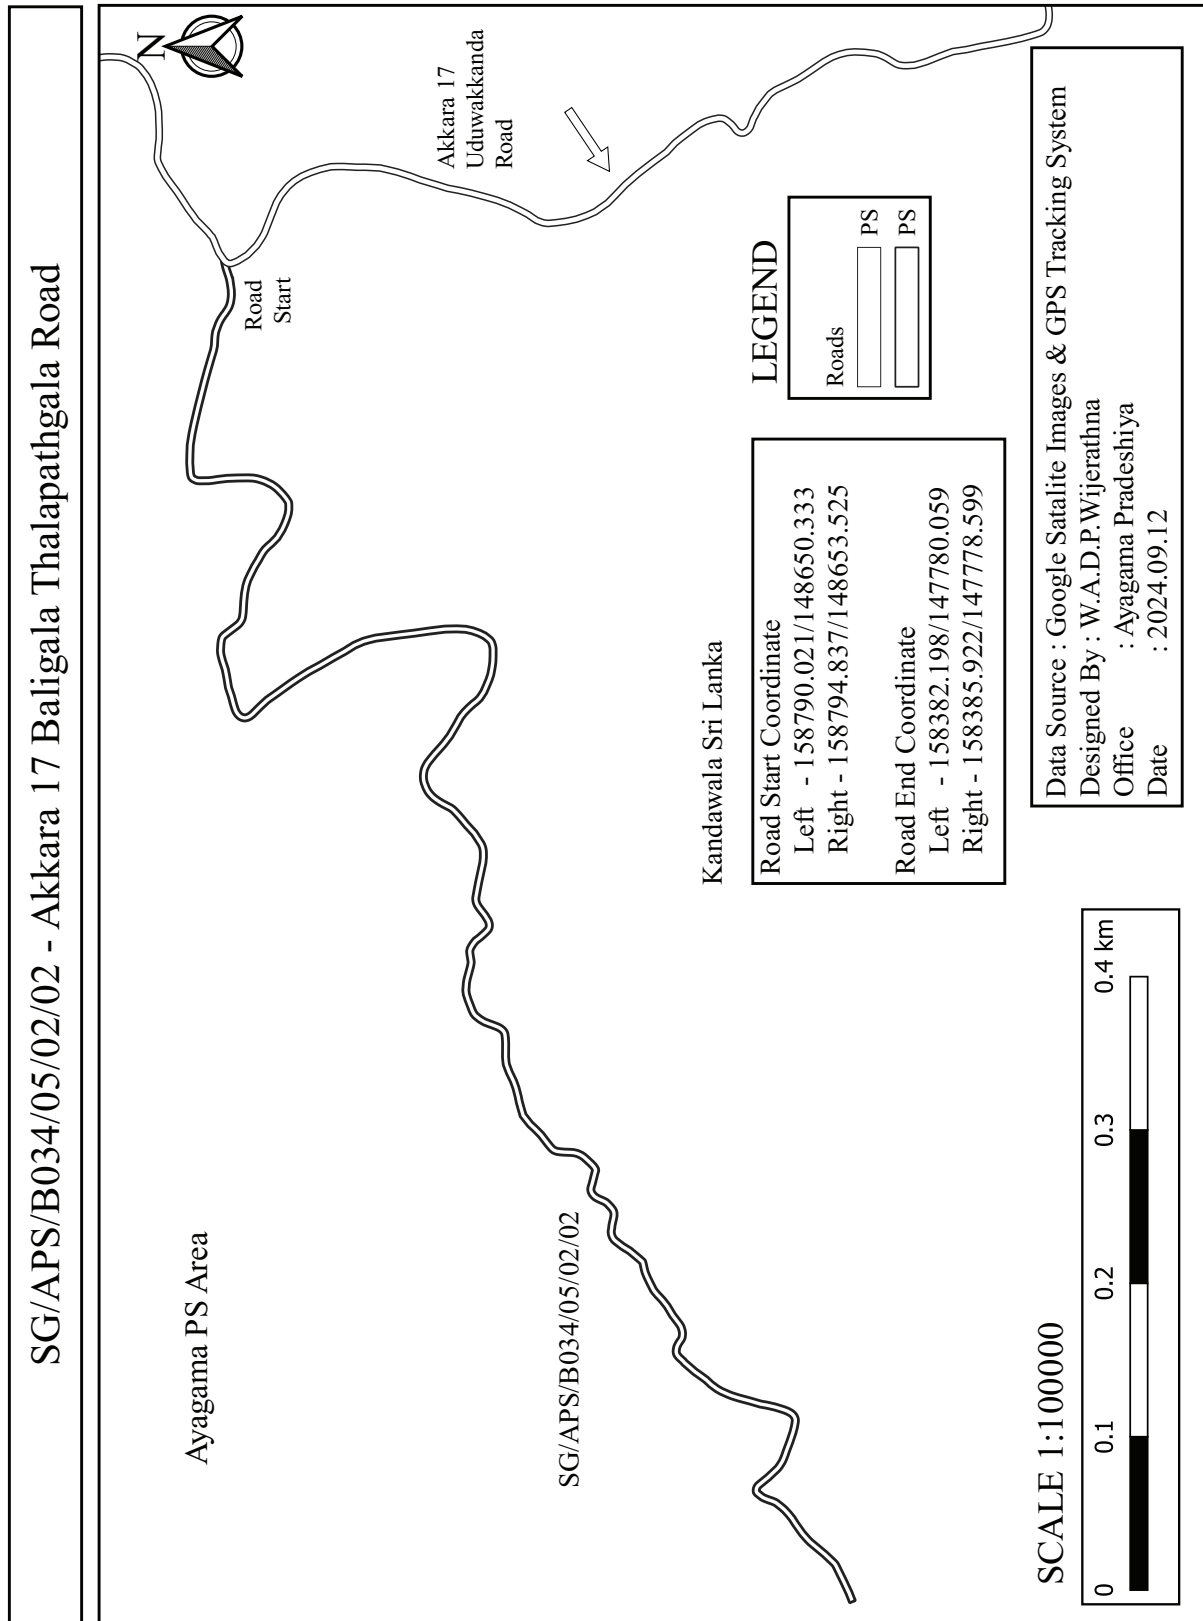


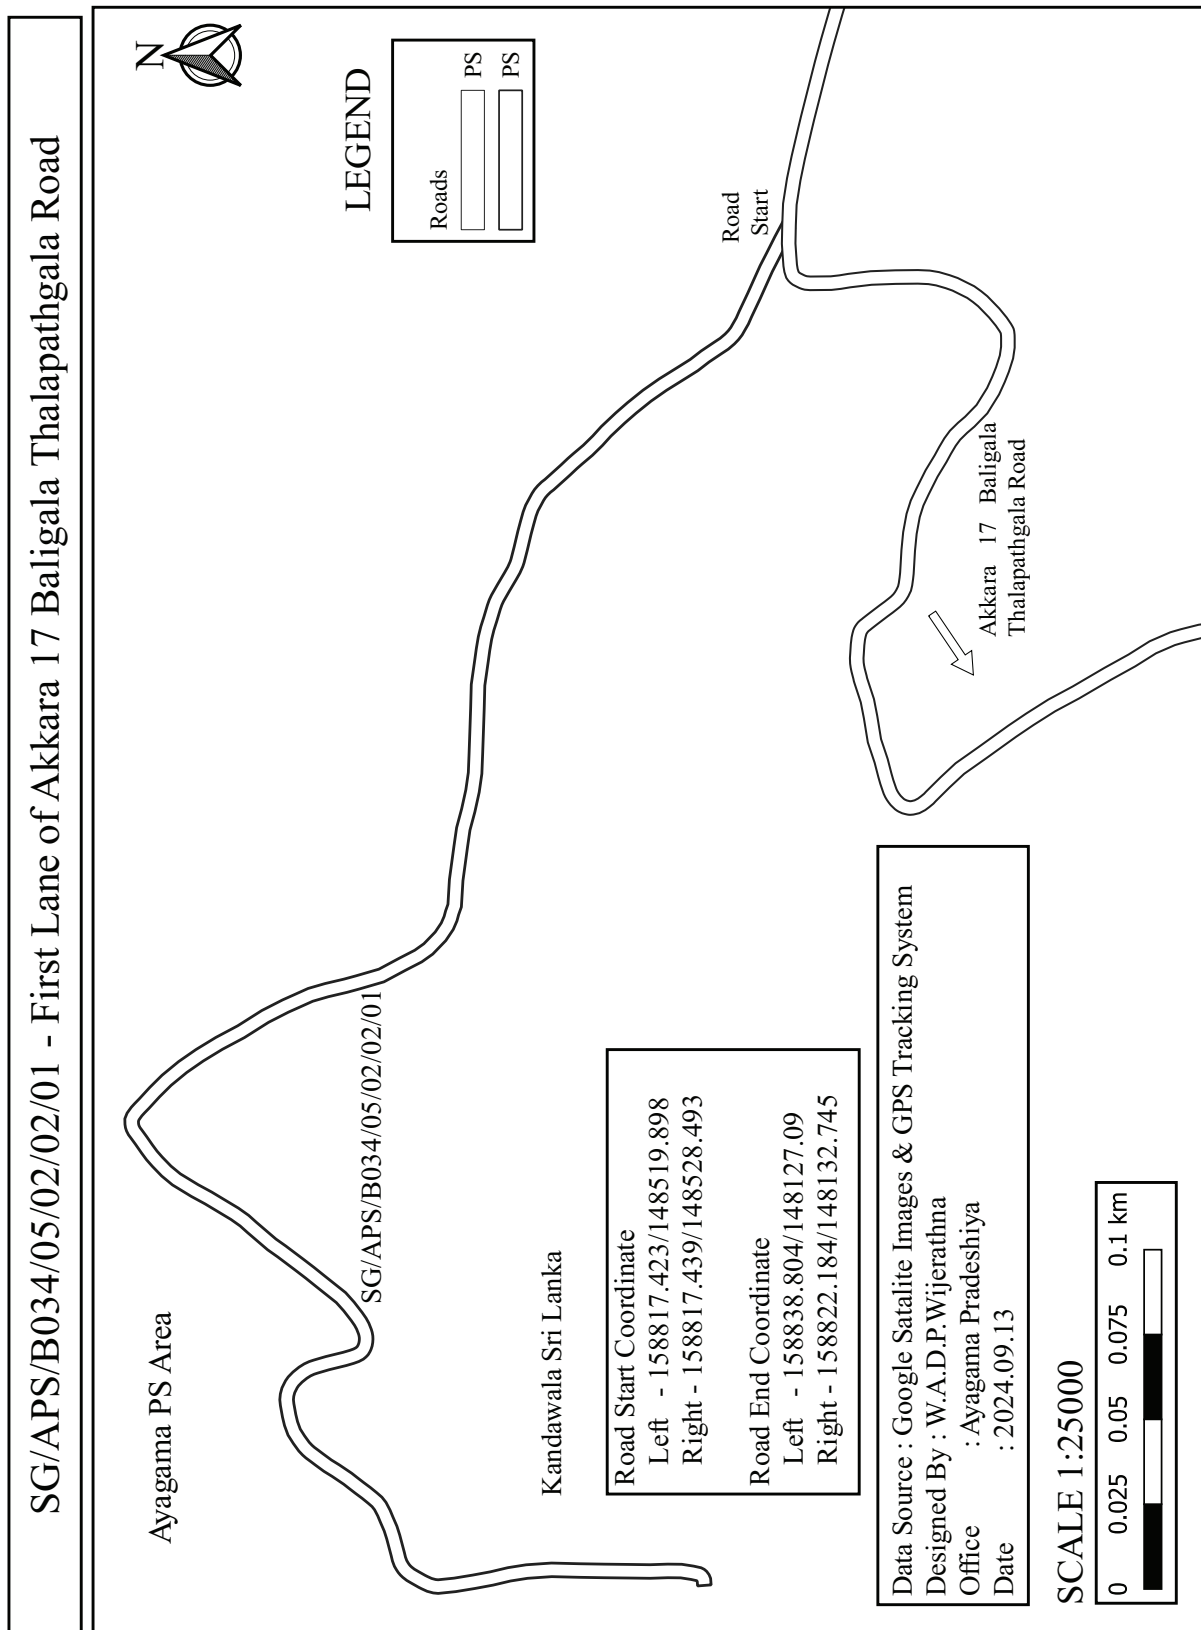


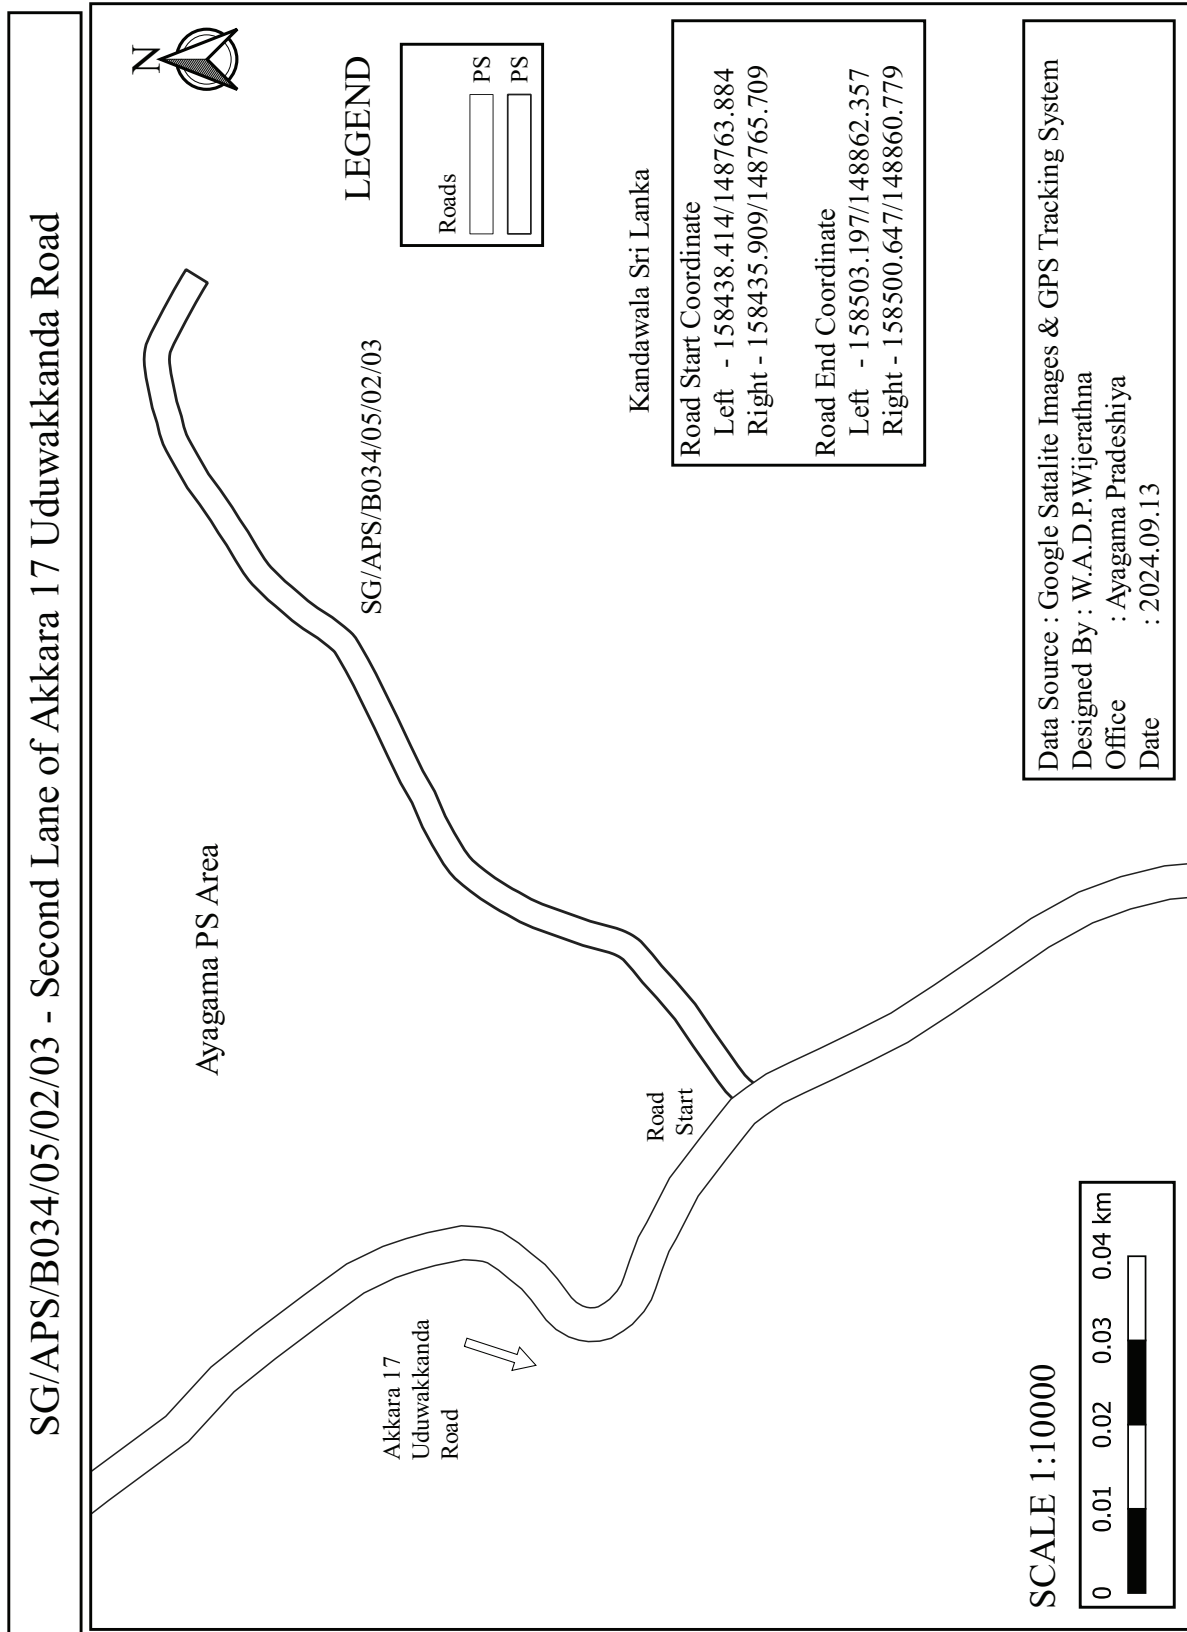








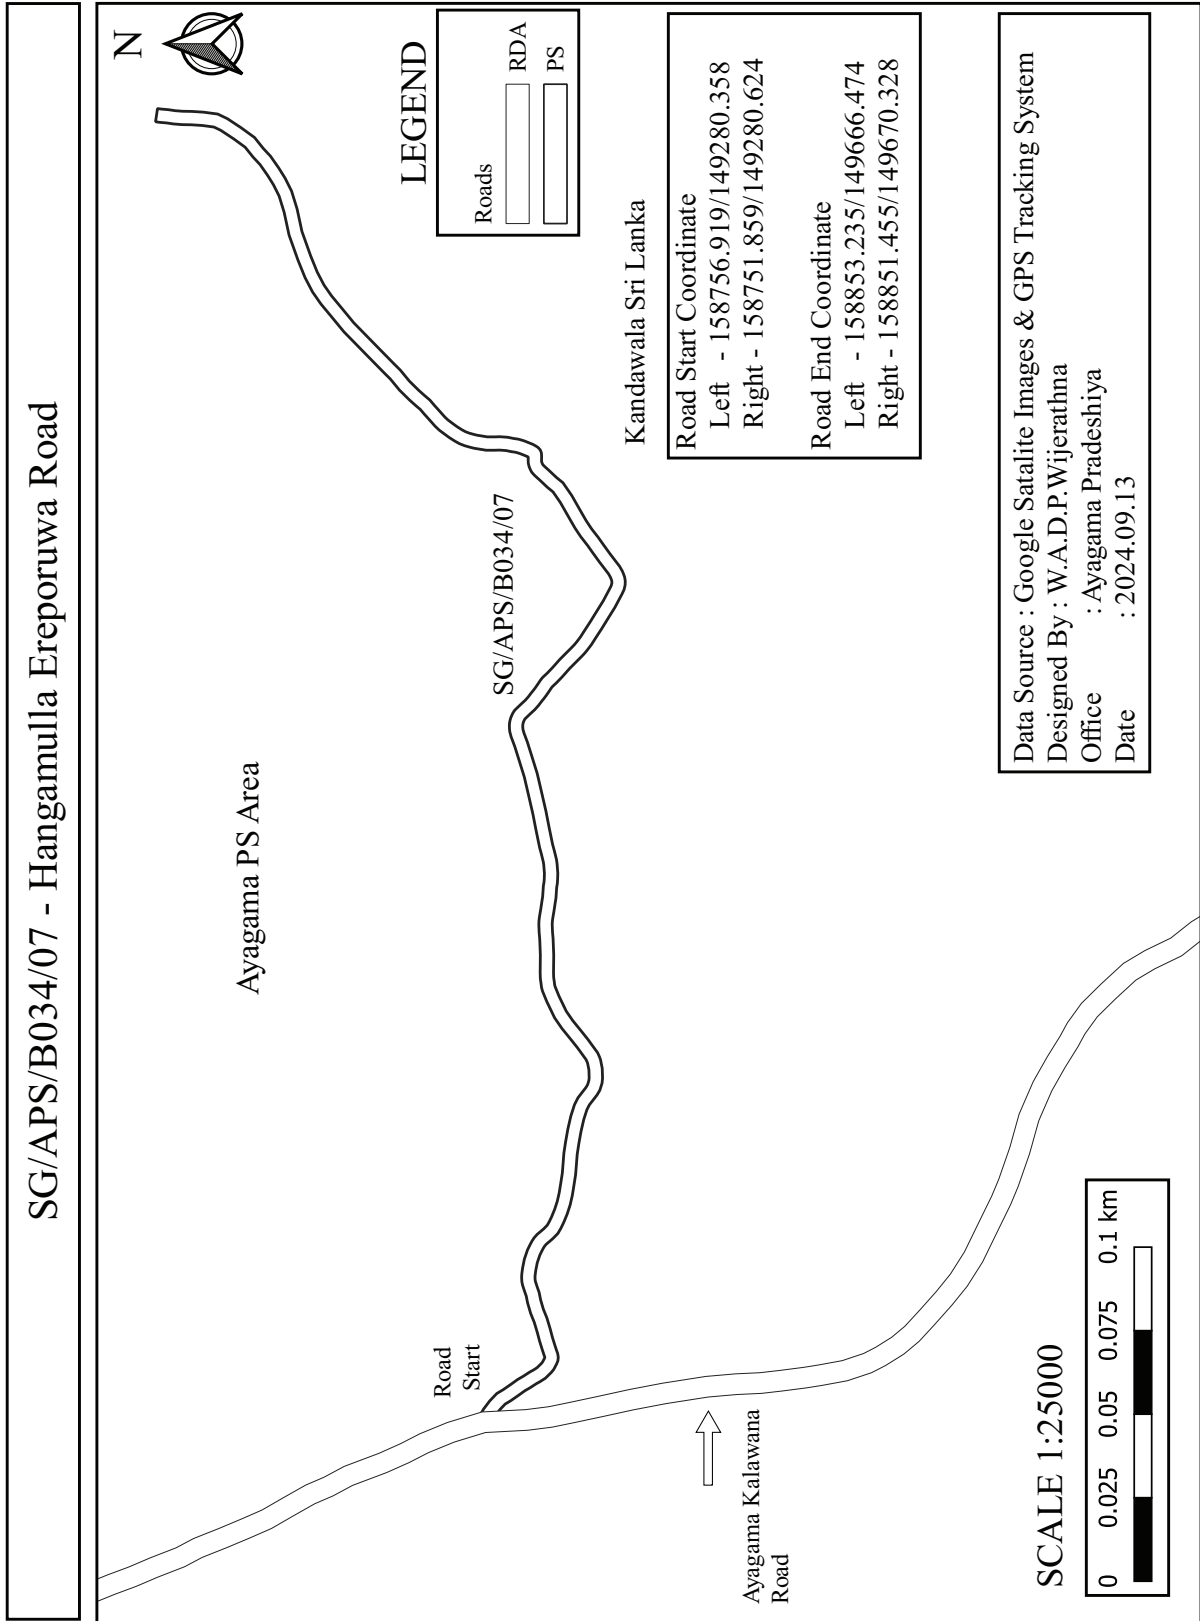


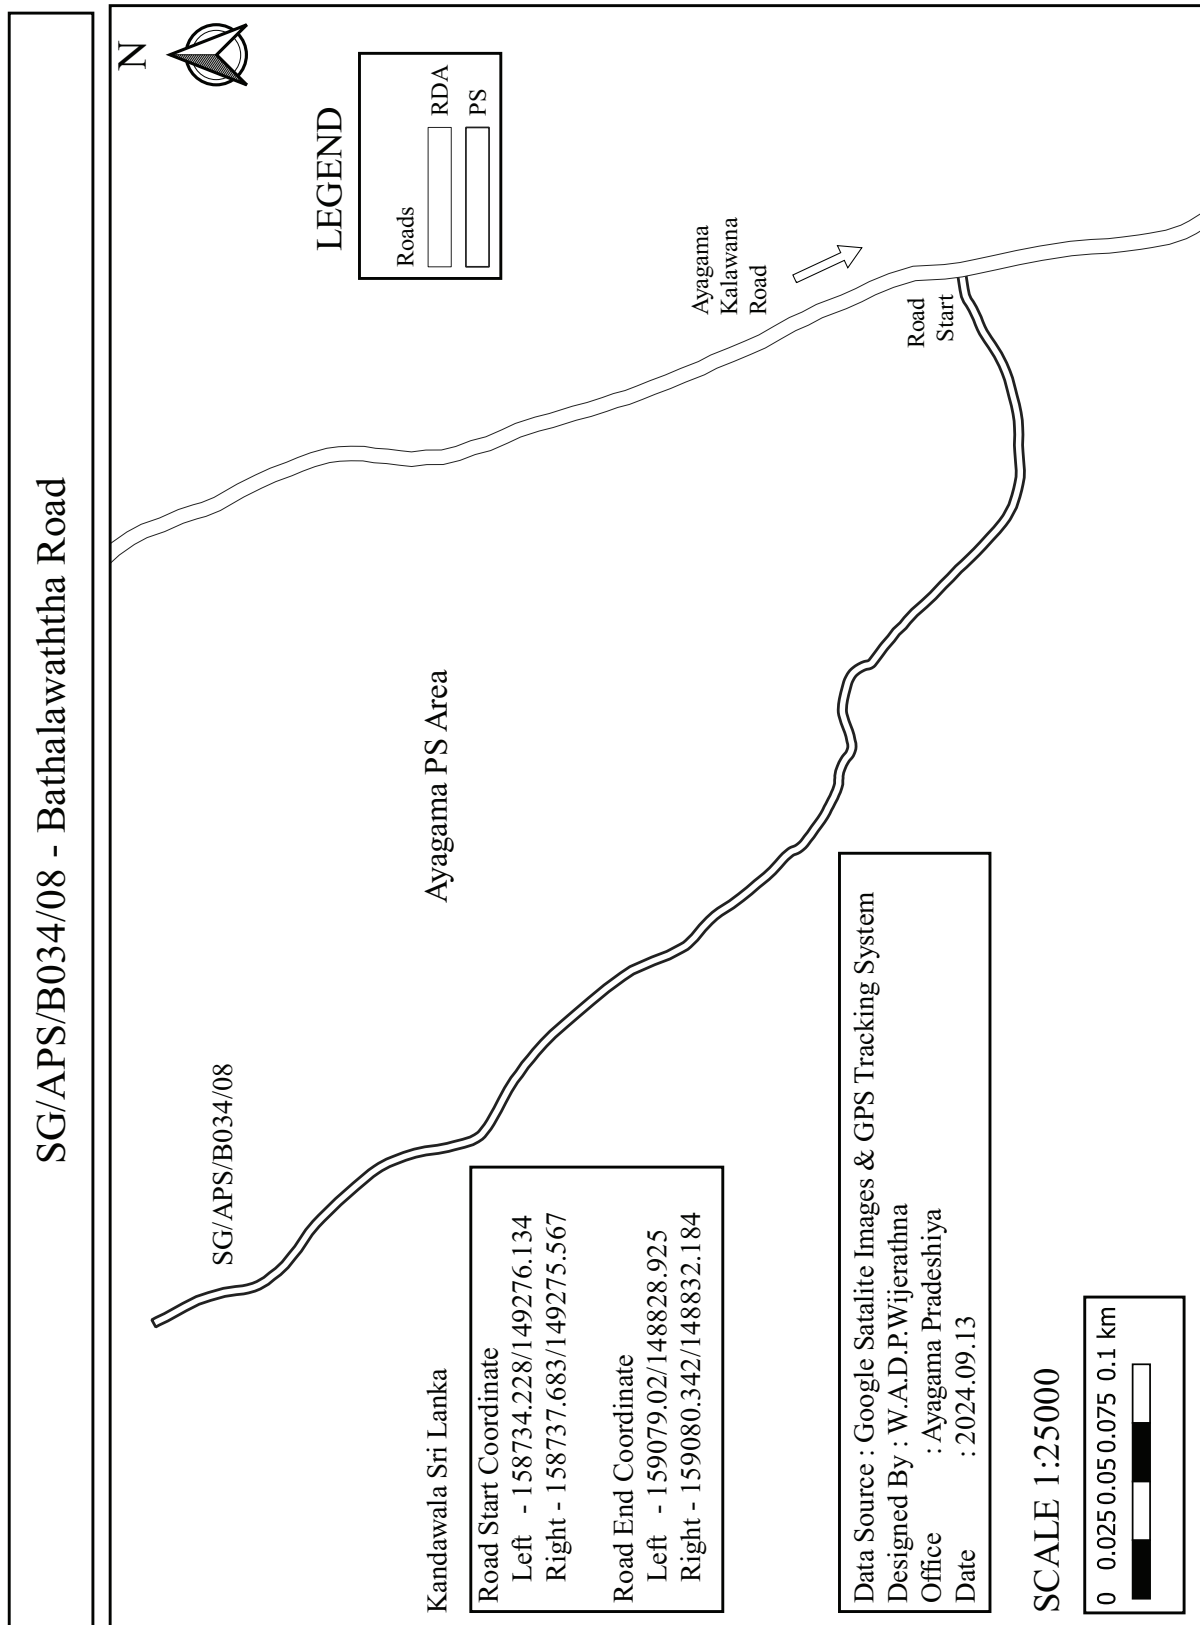

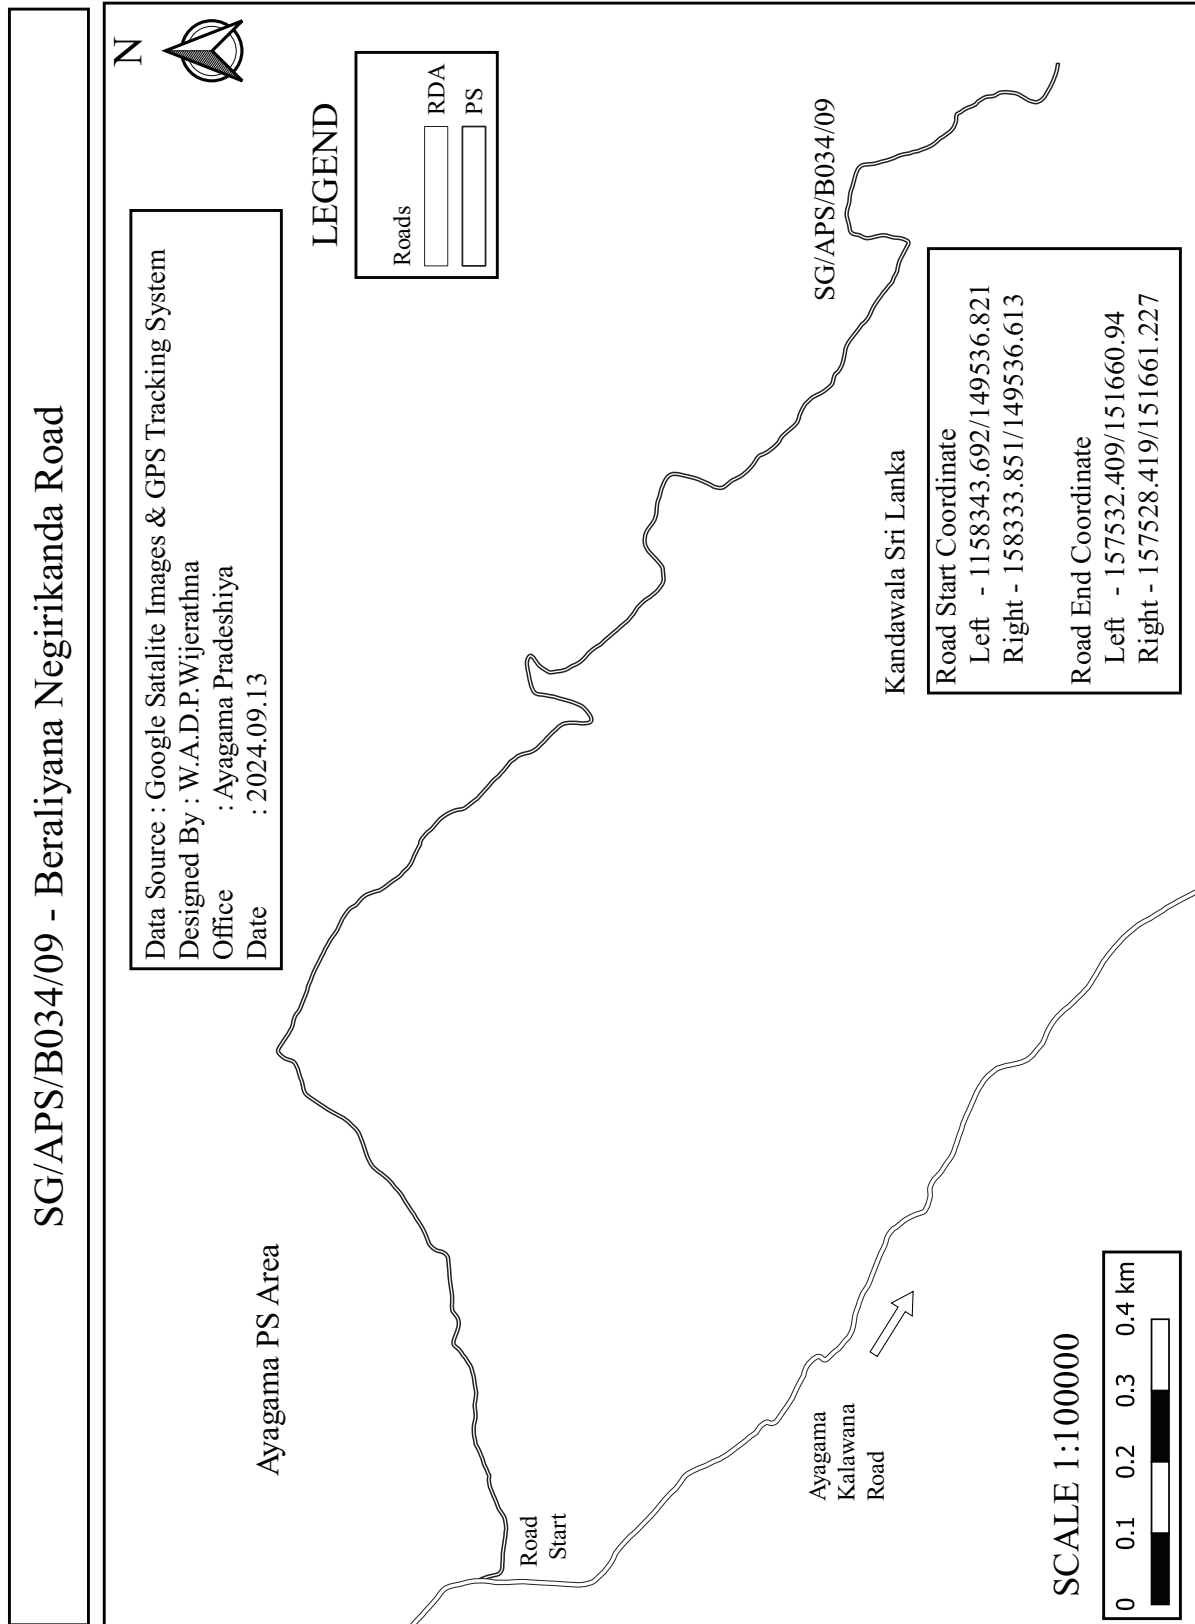


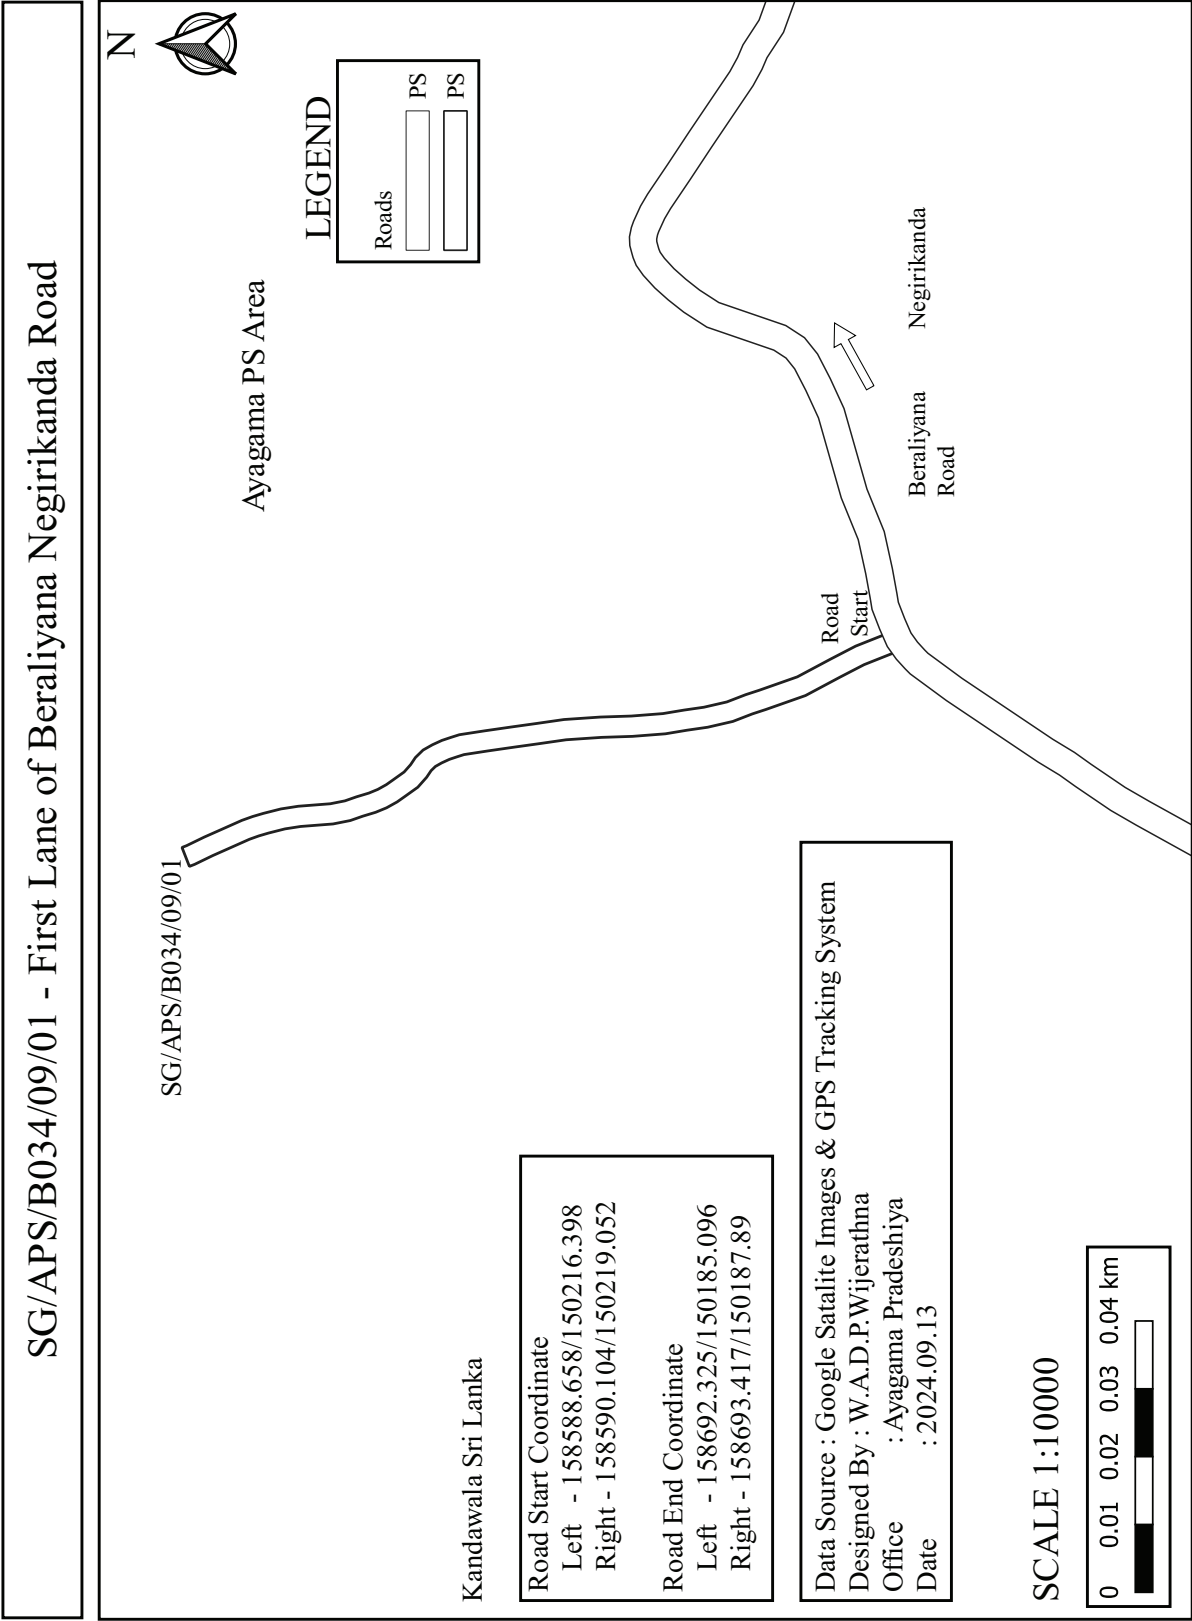


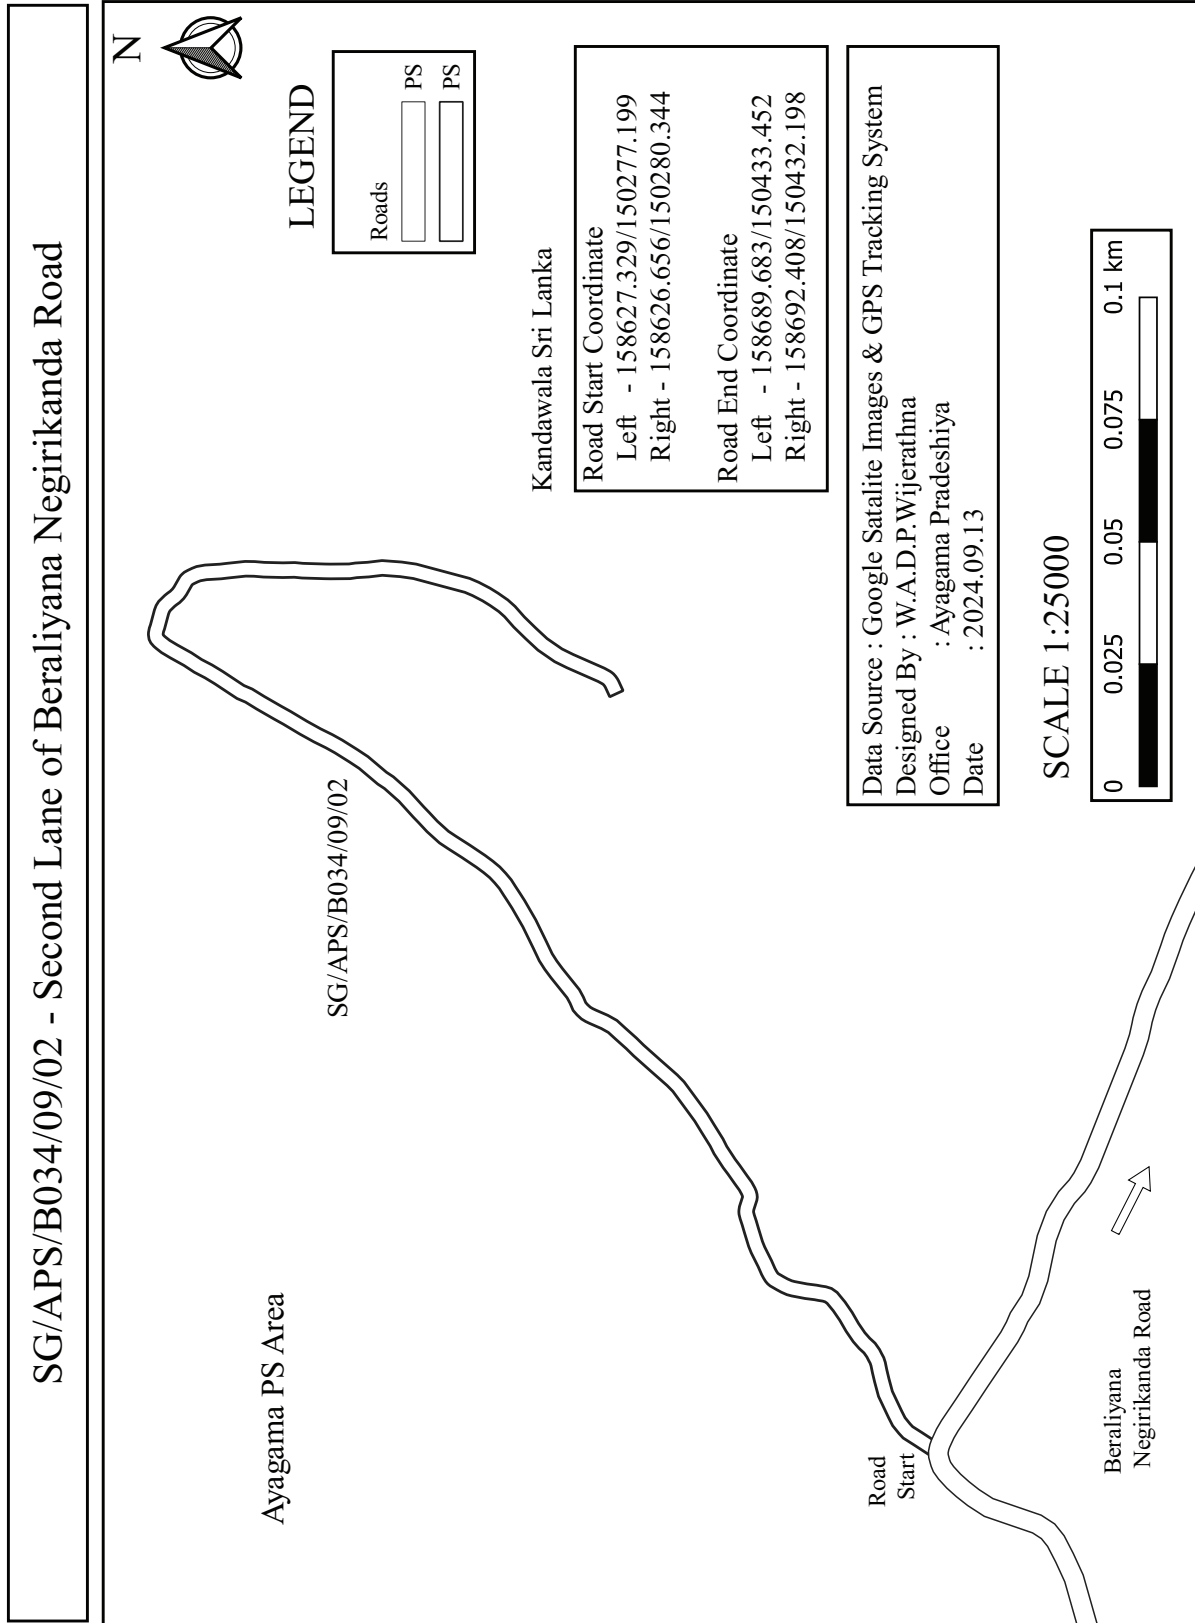

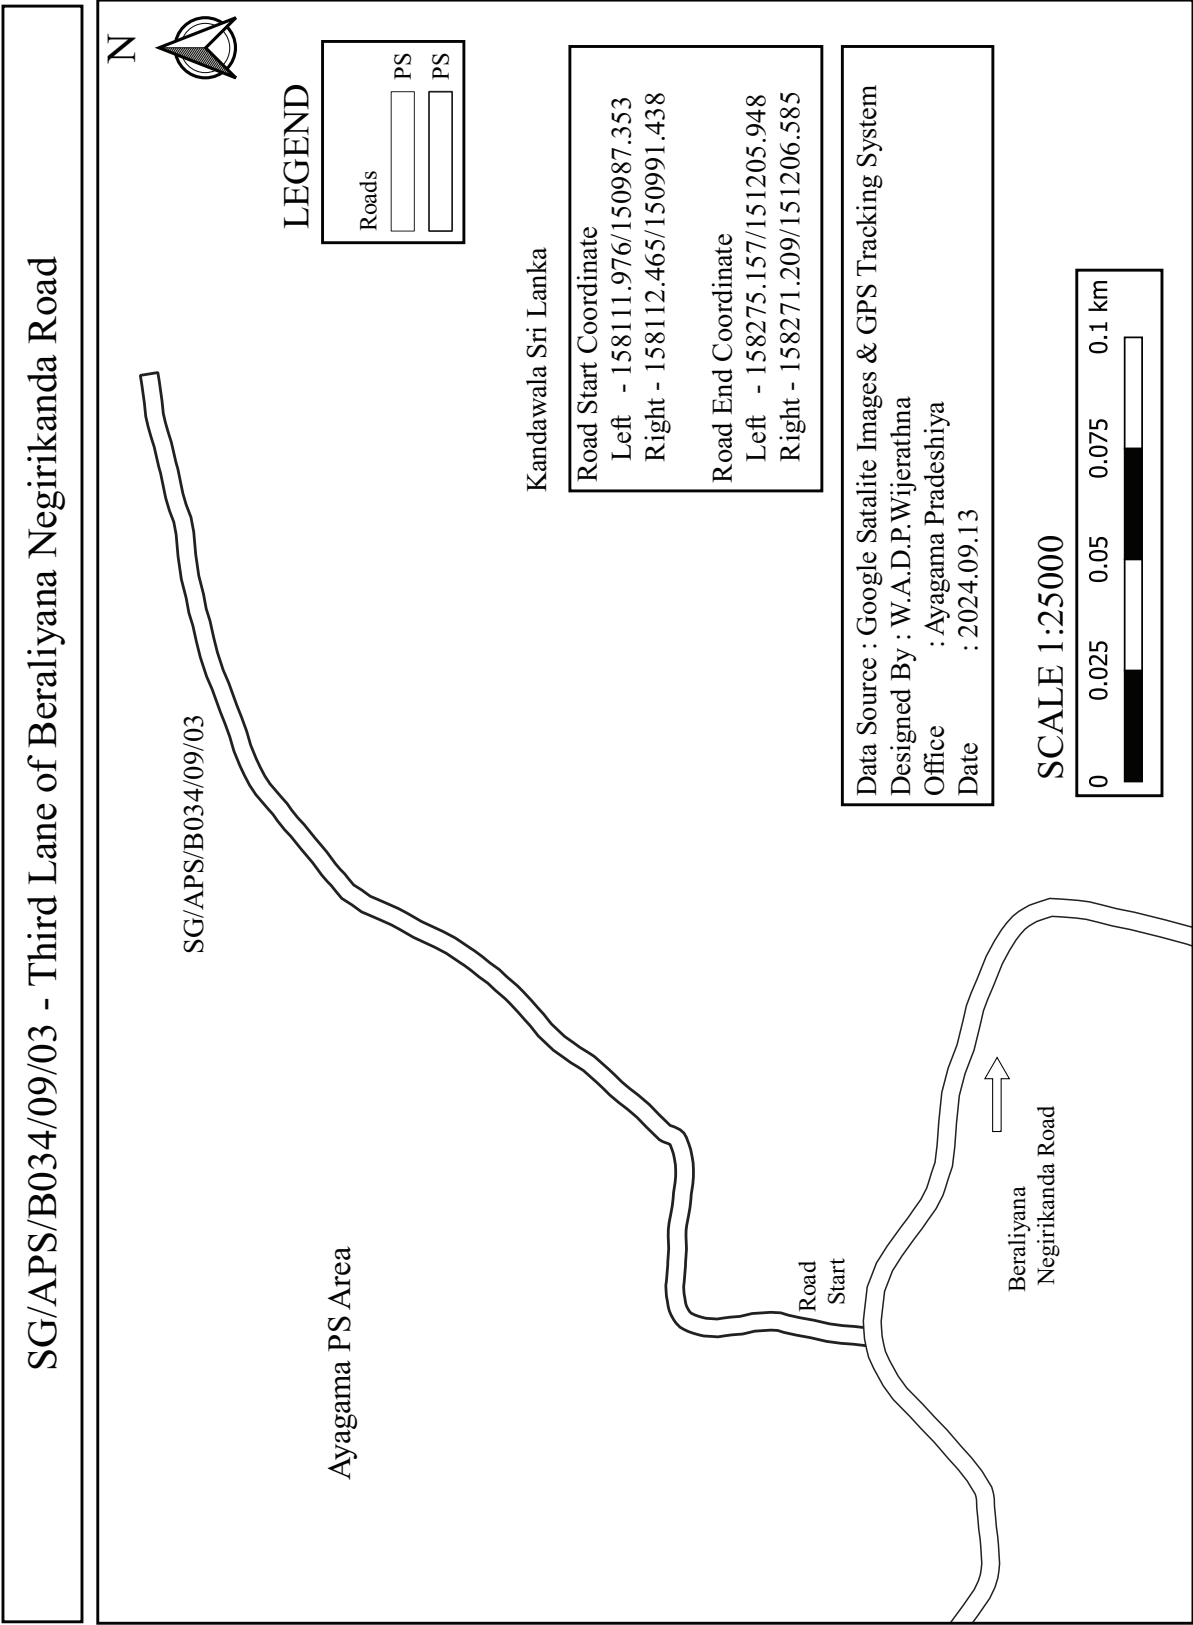



SG/APS/B034/09/03/01 - First By Pass of Third Lane of Beraliyana Negirikanda Road

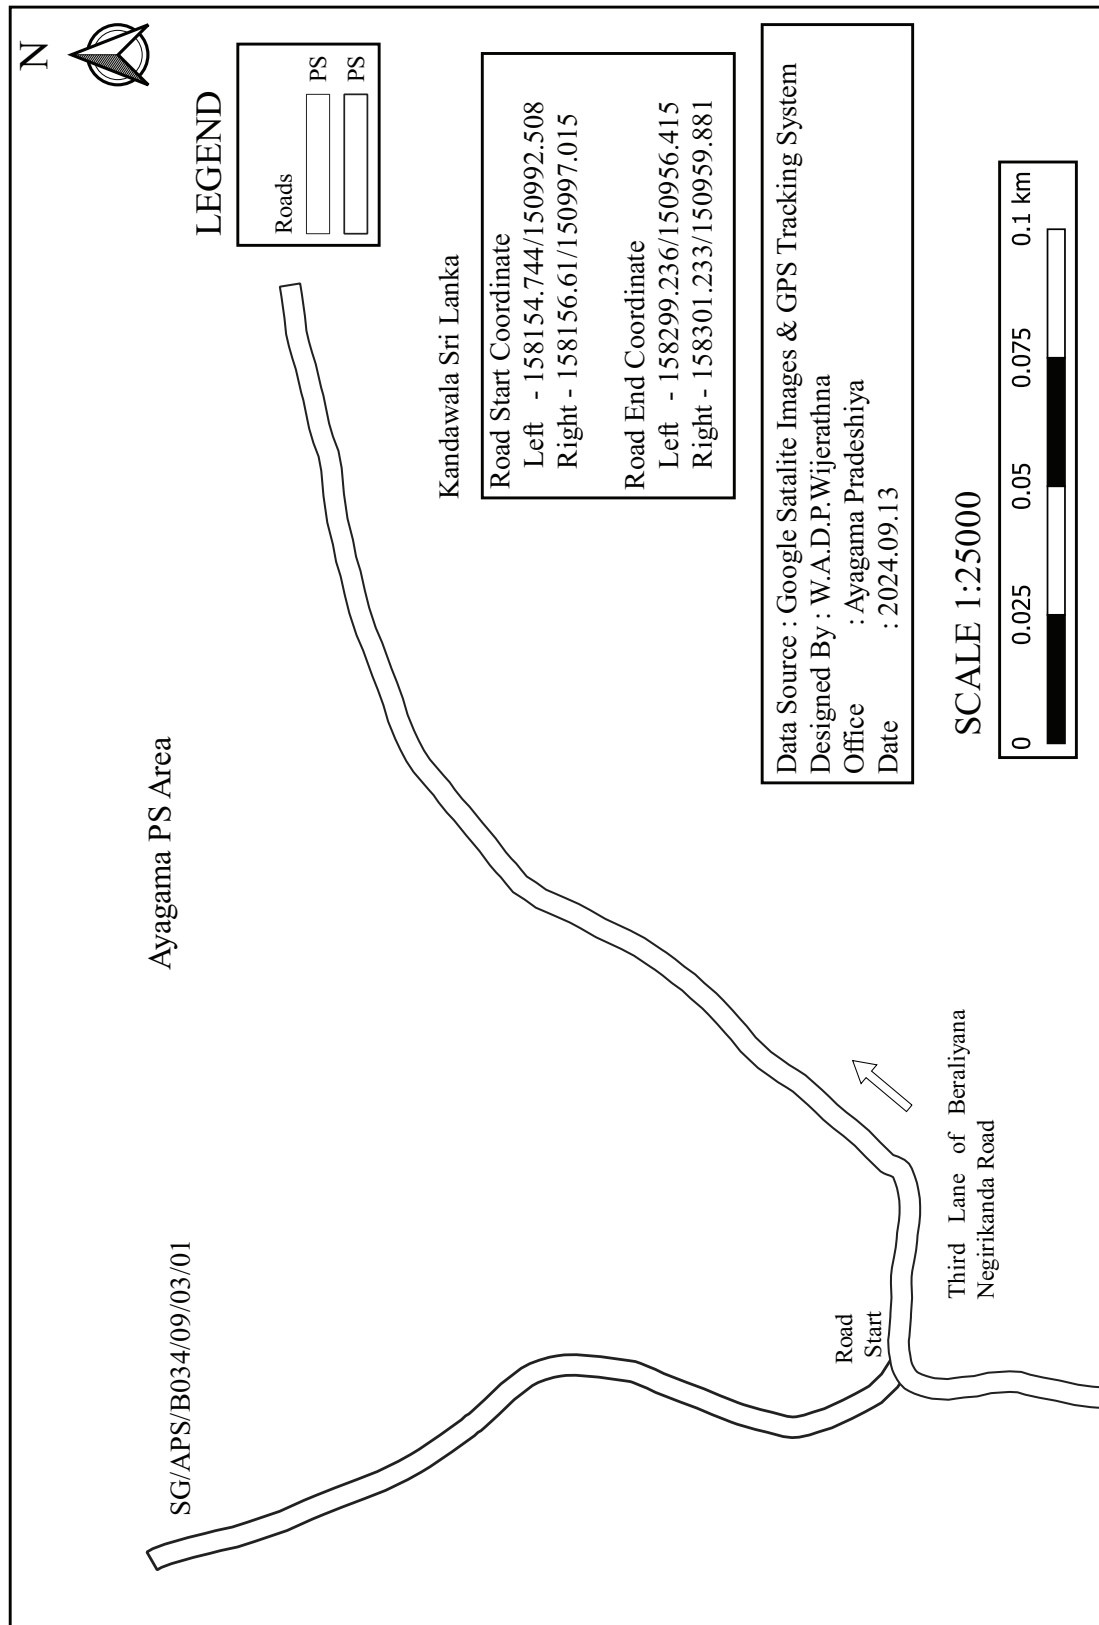


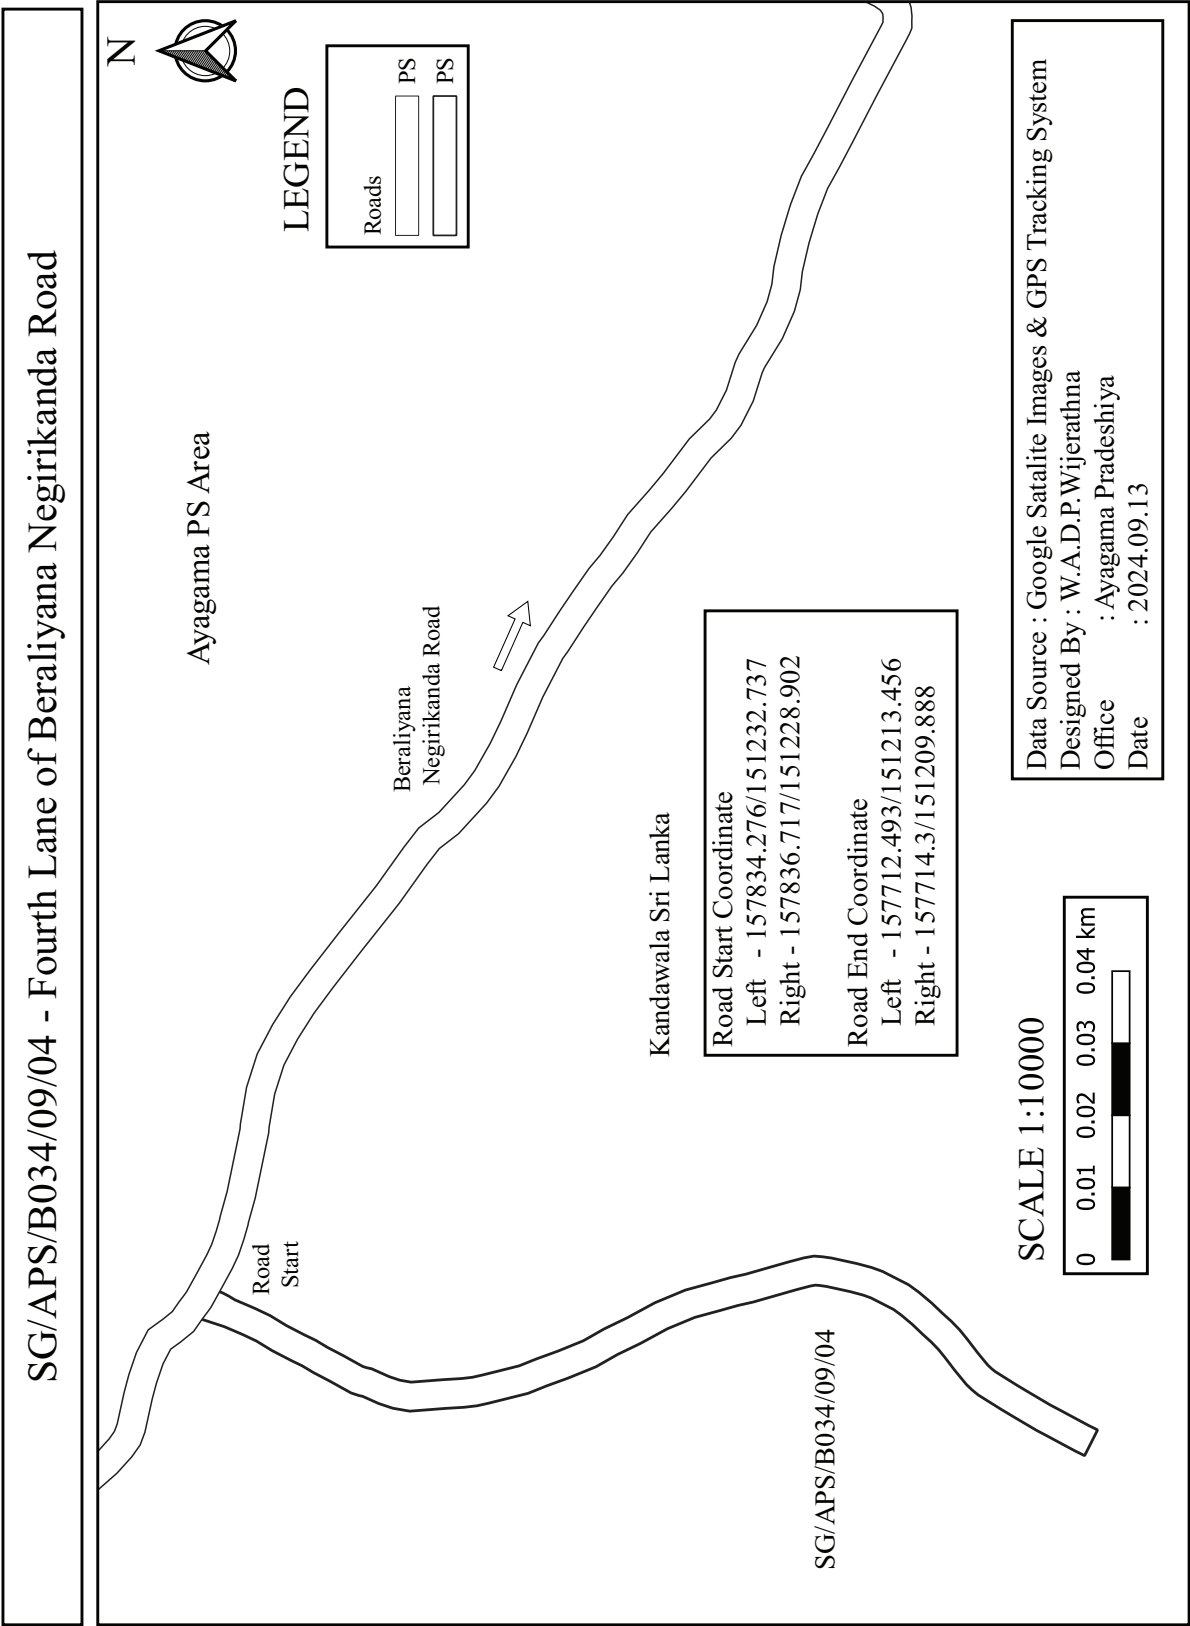





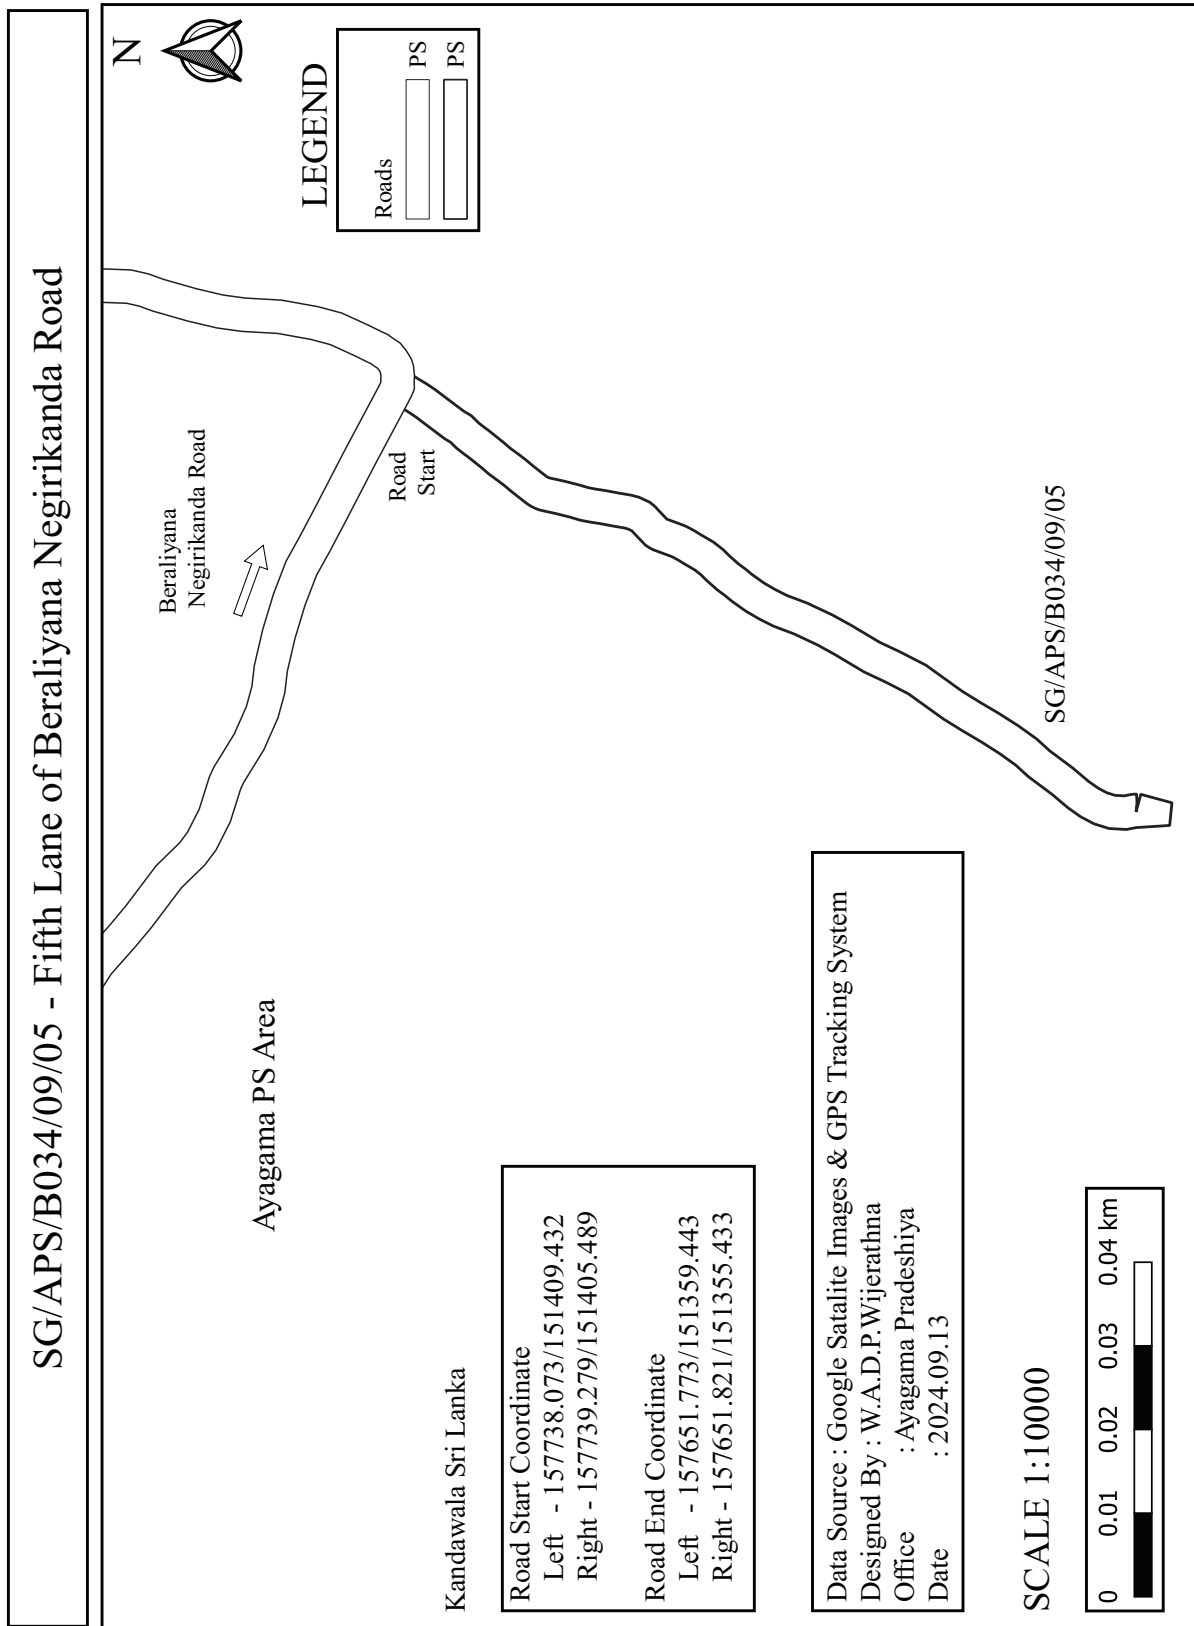


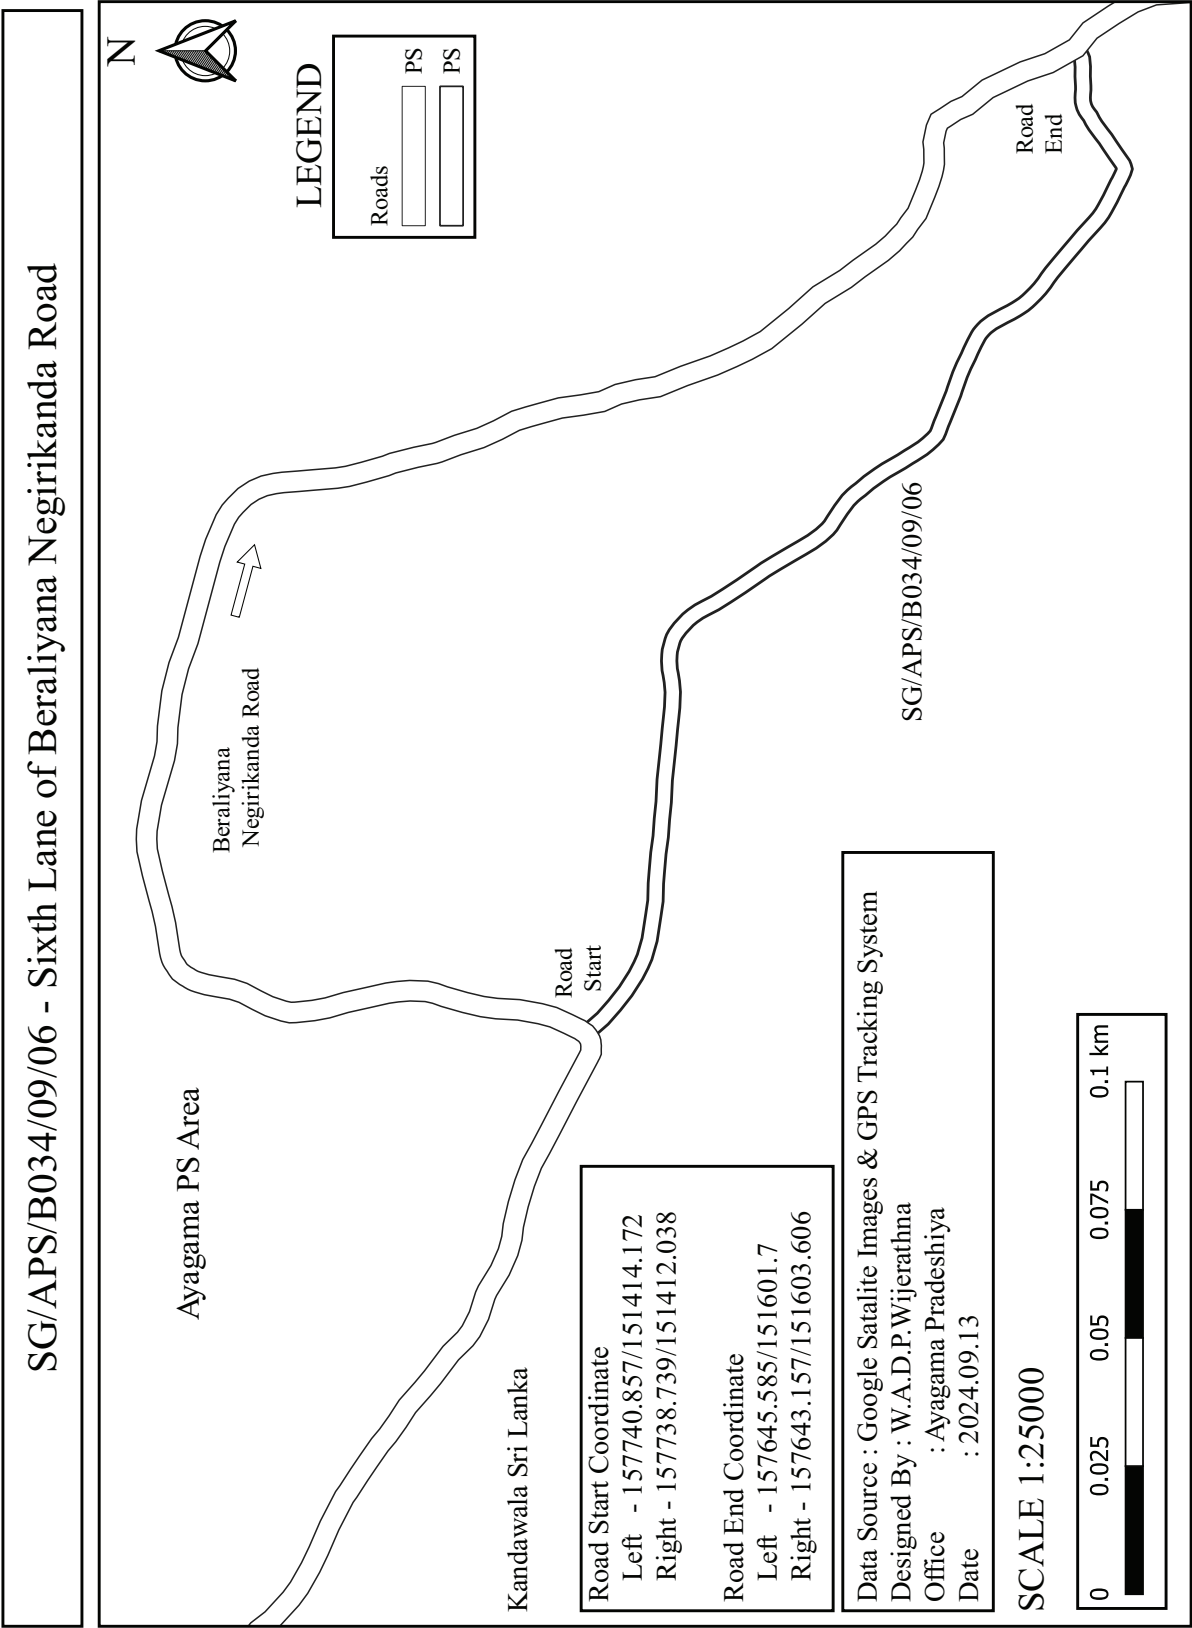


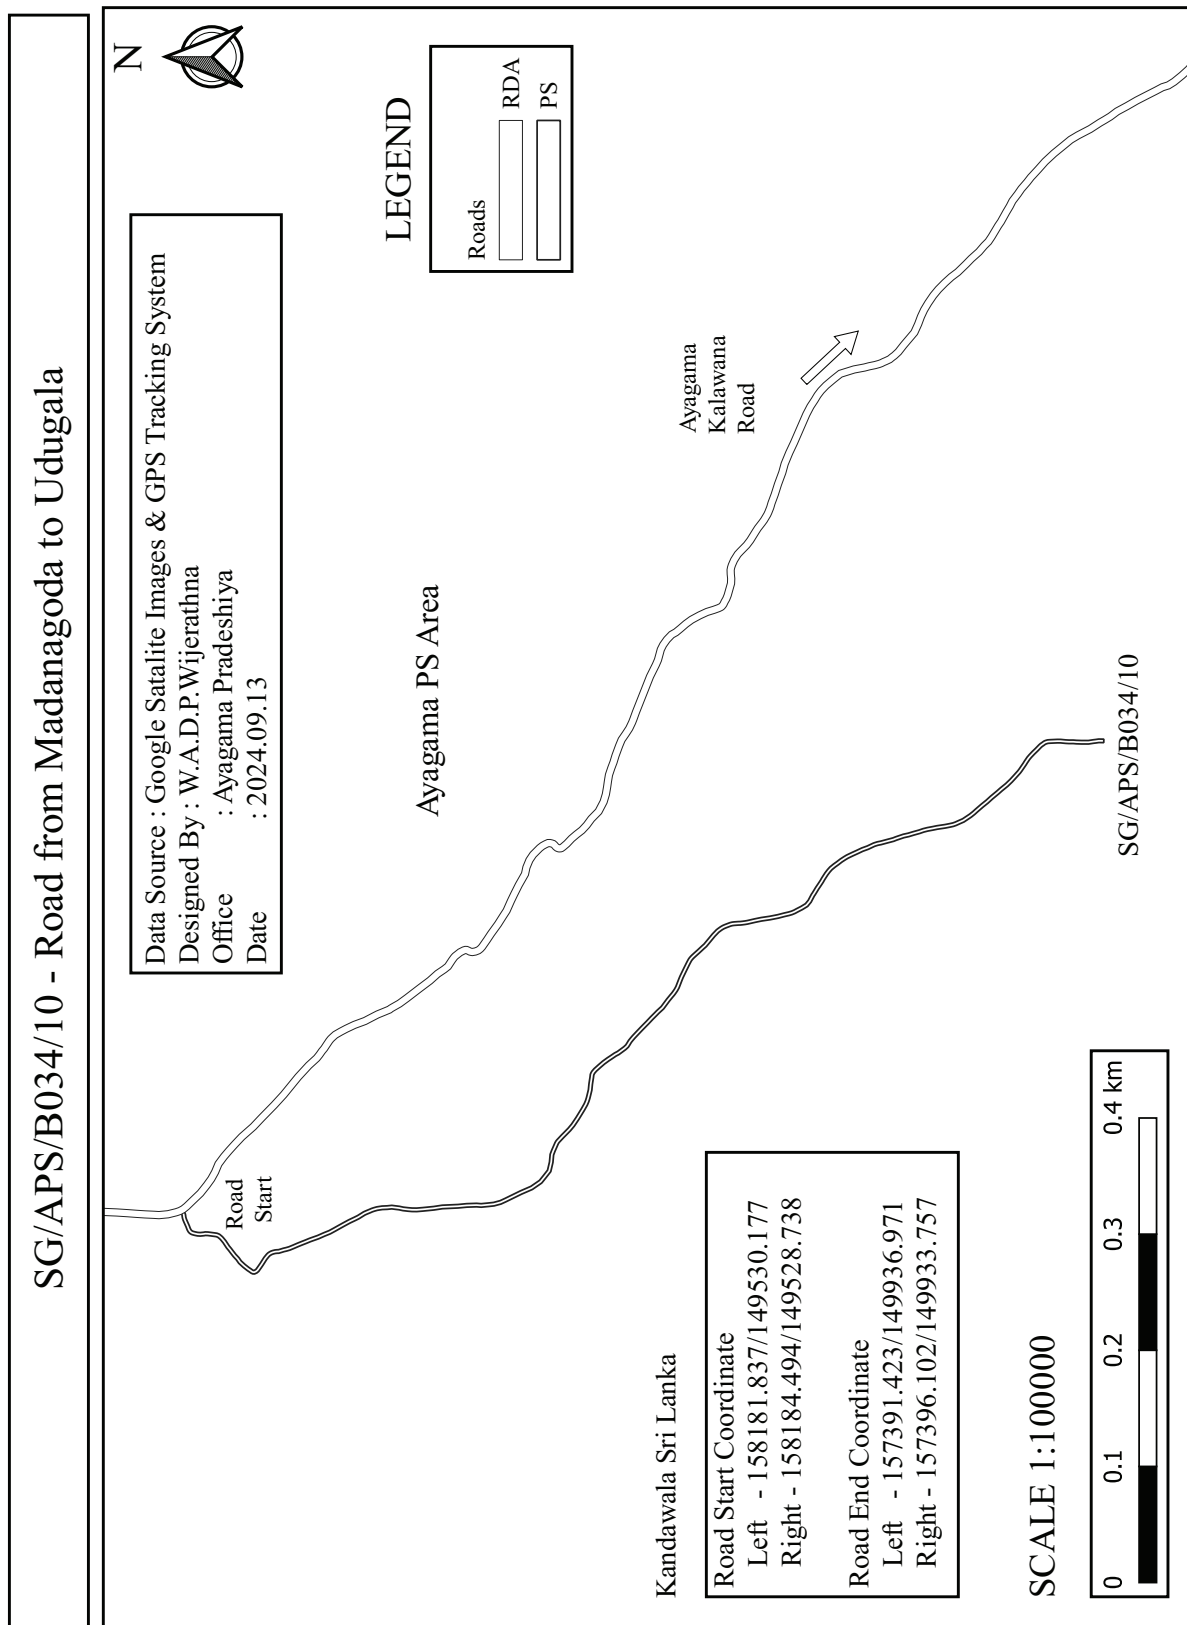


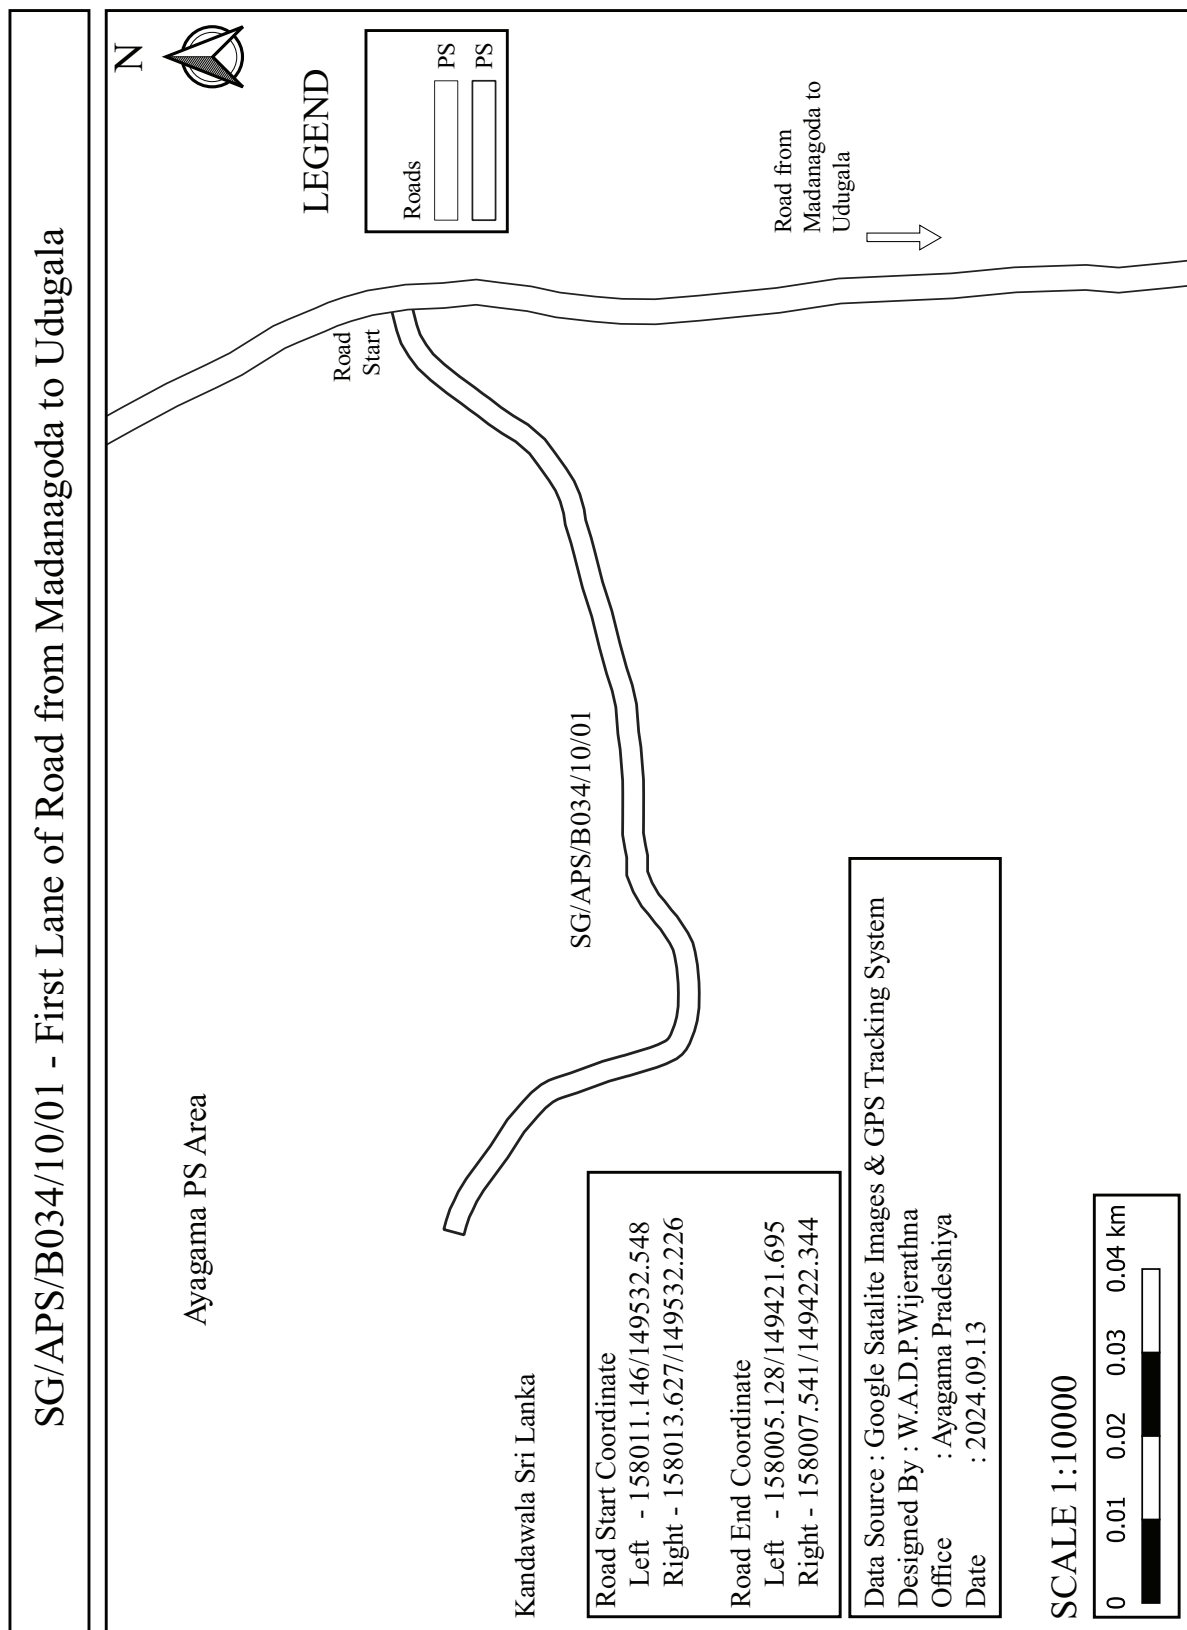

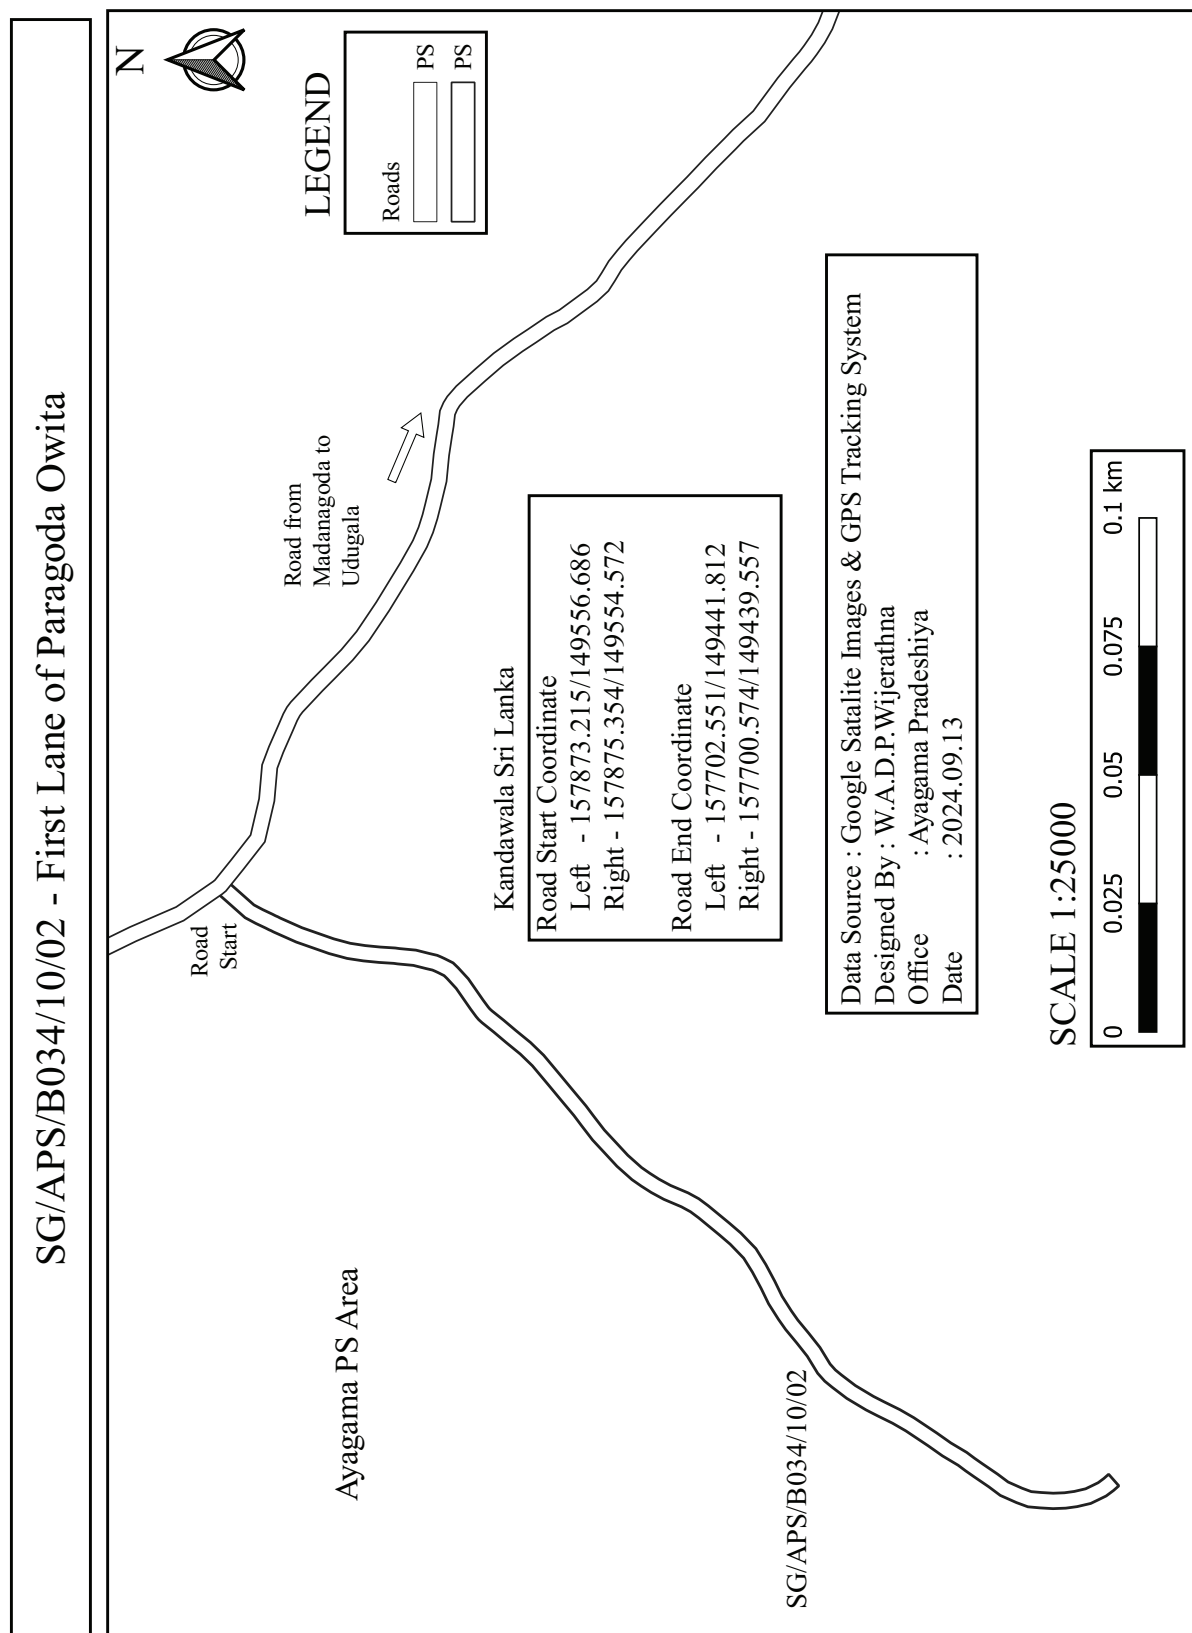


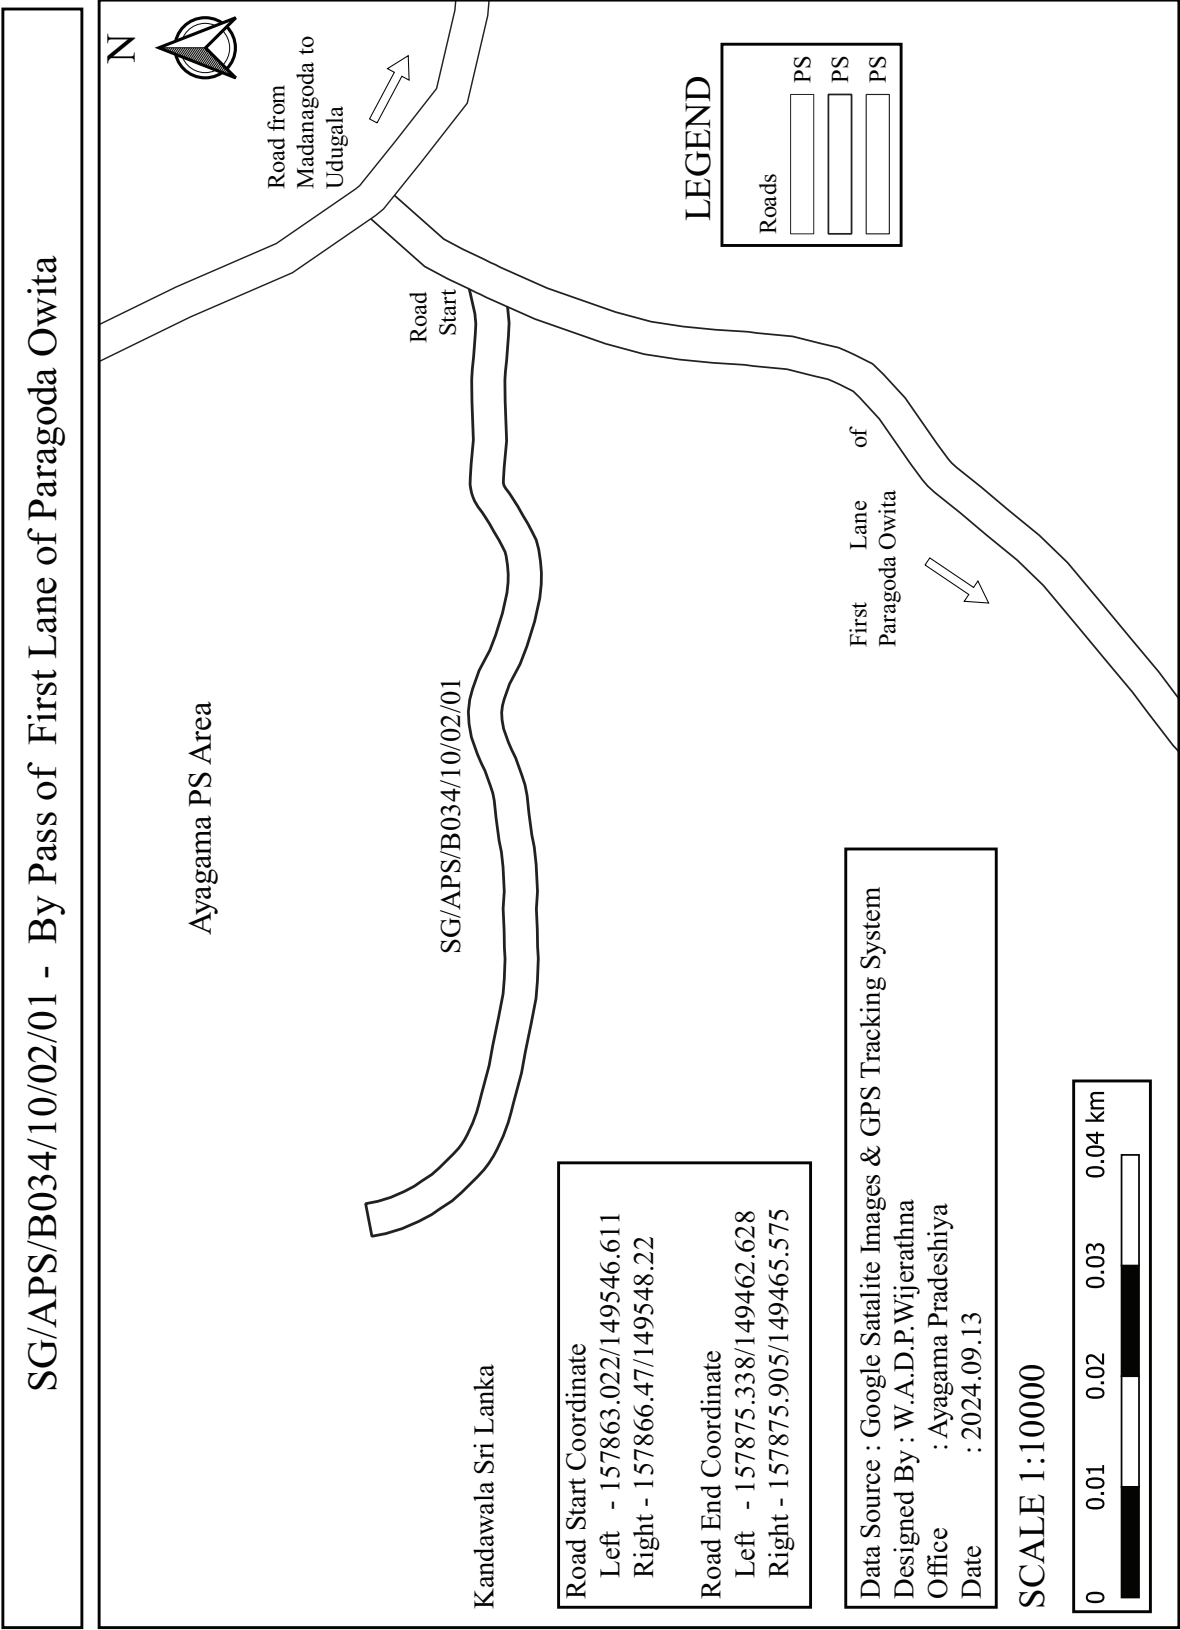


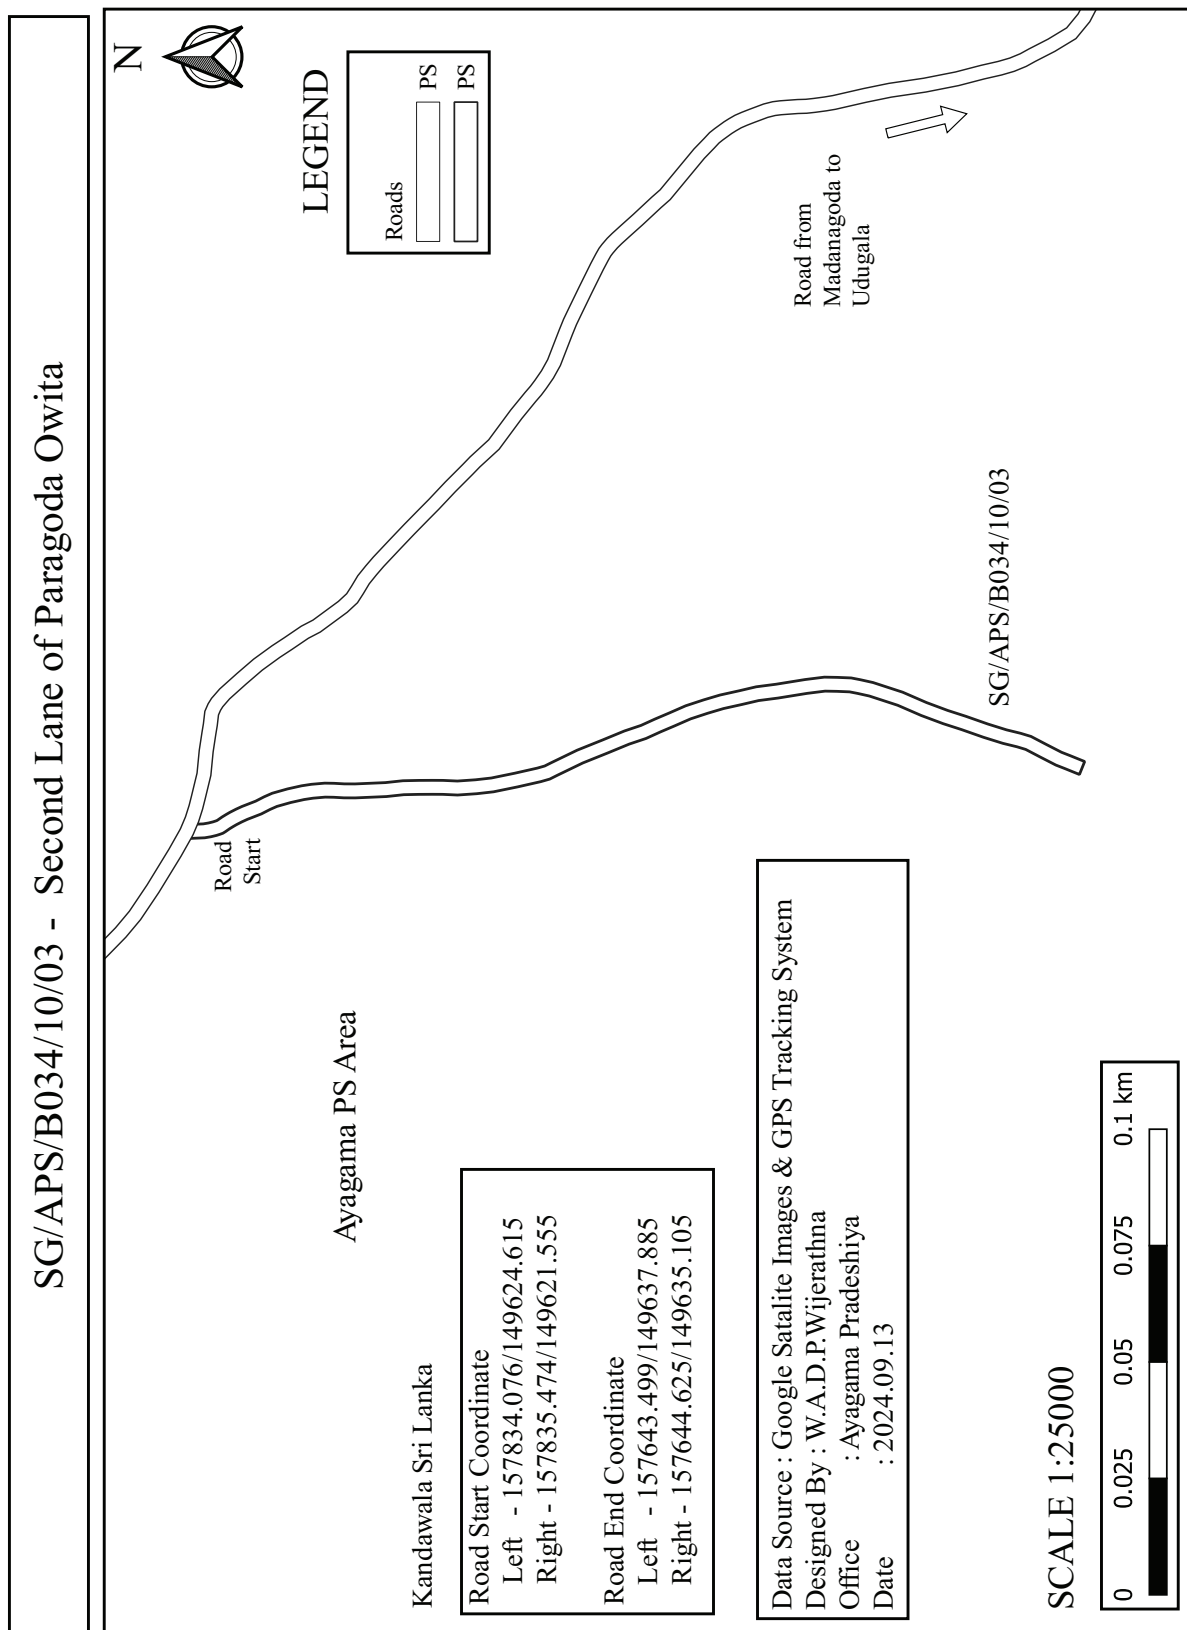


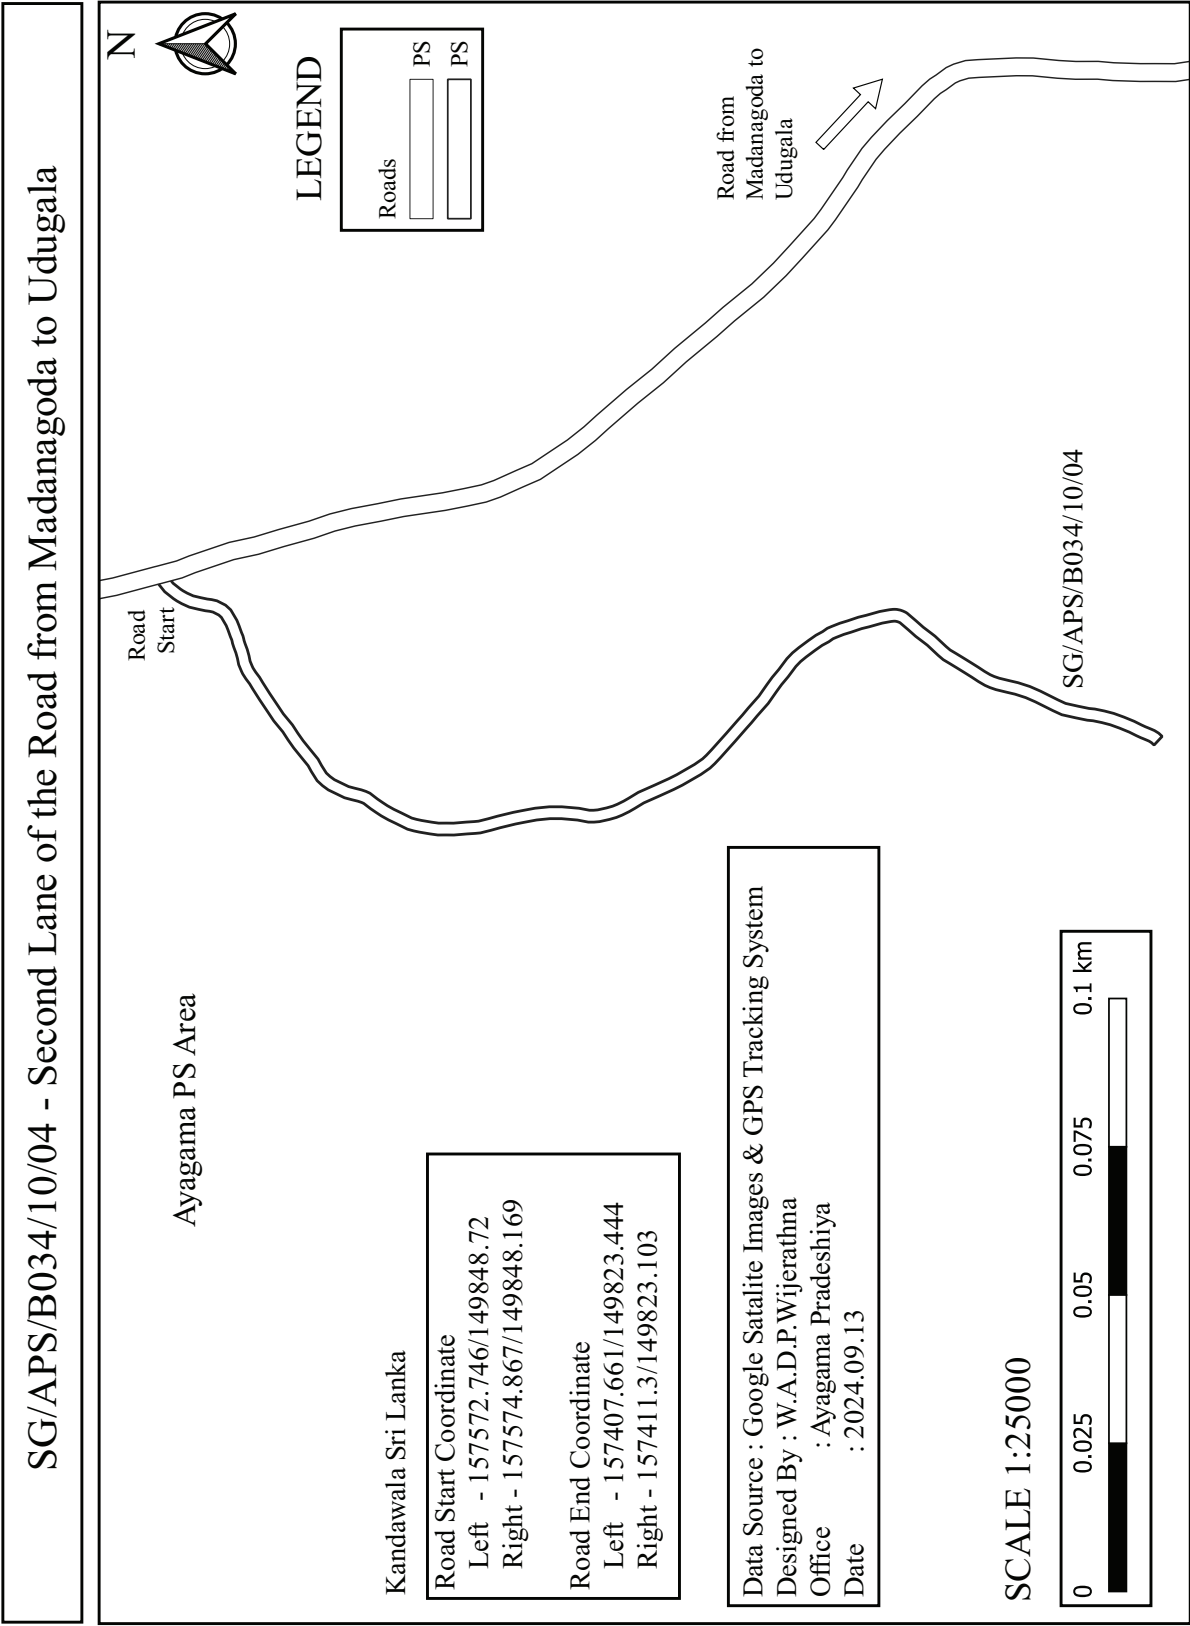





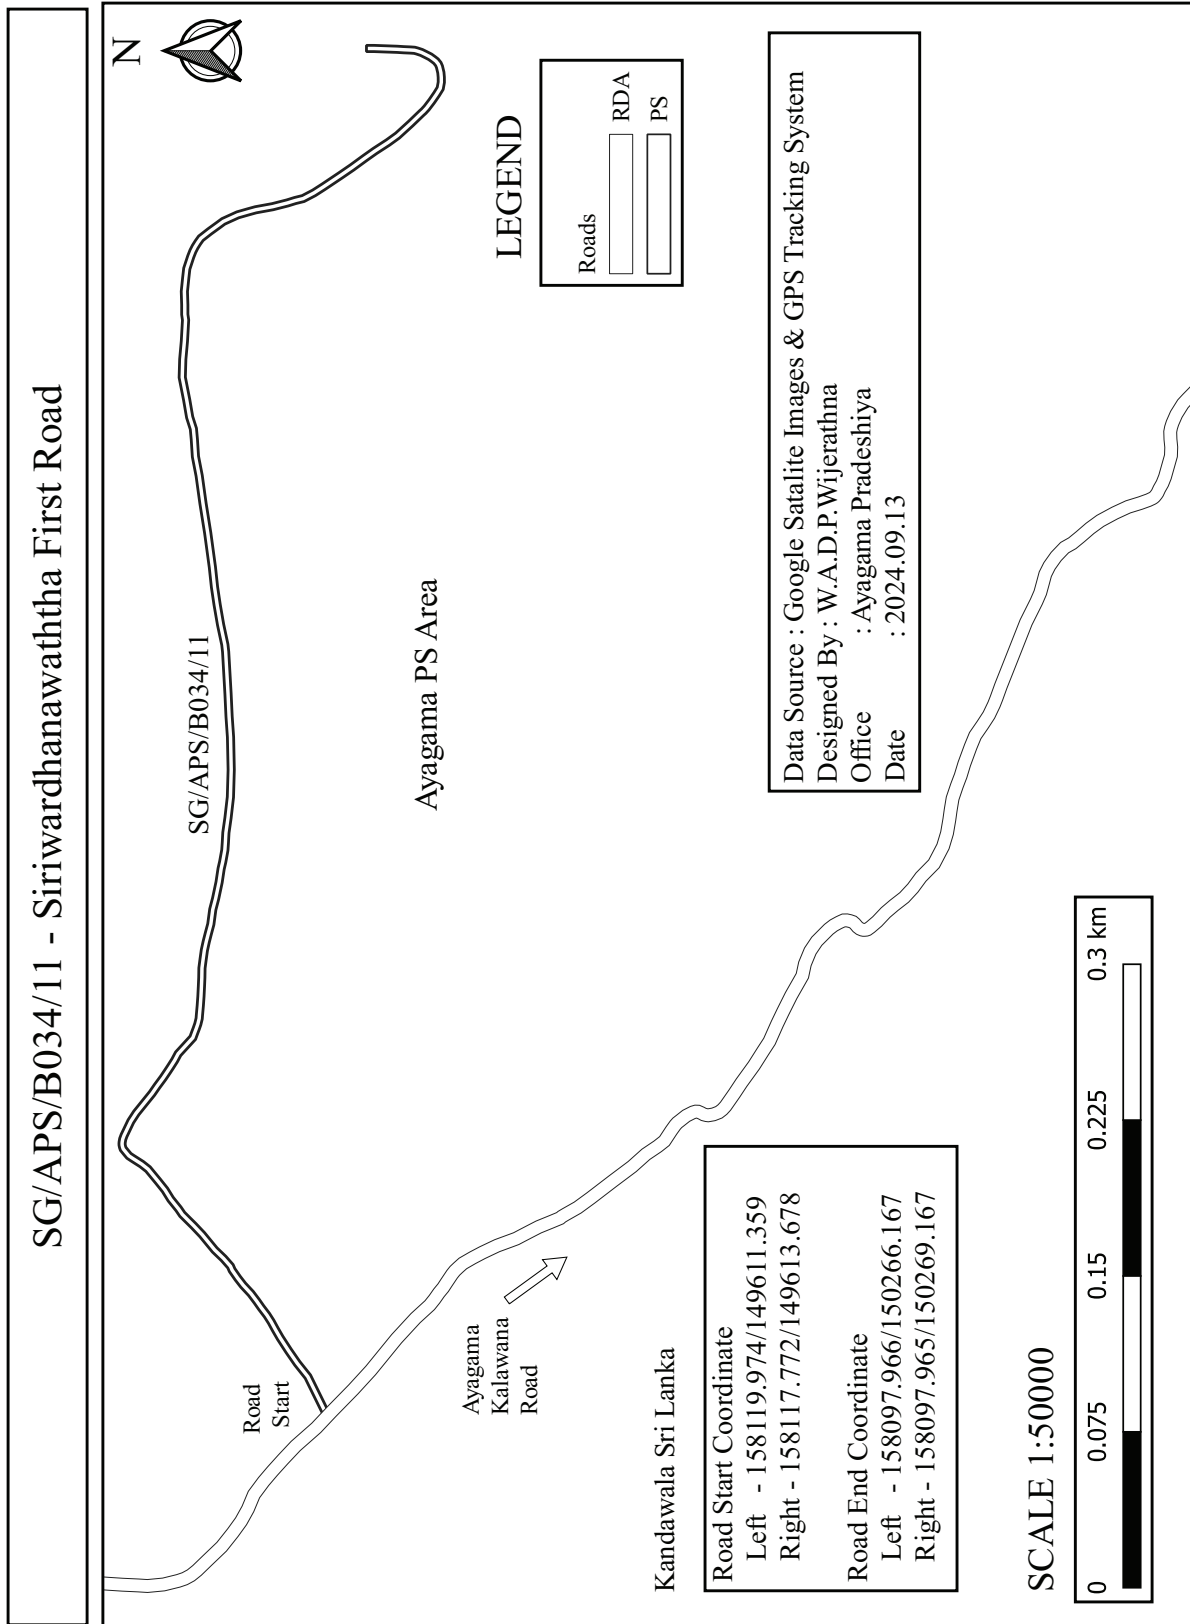


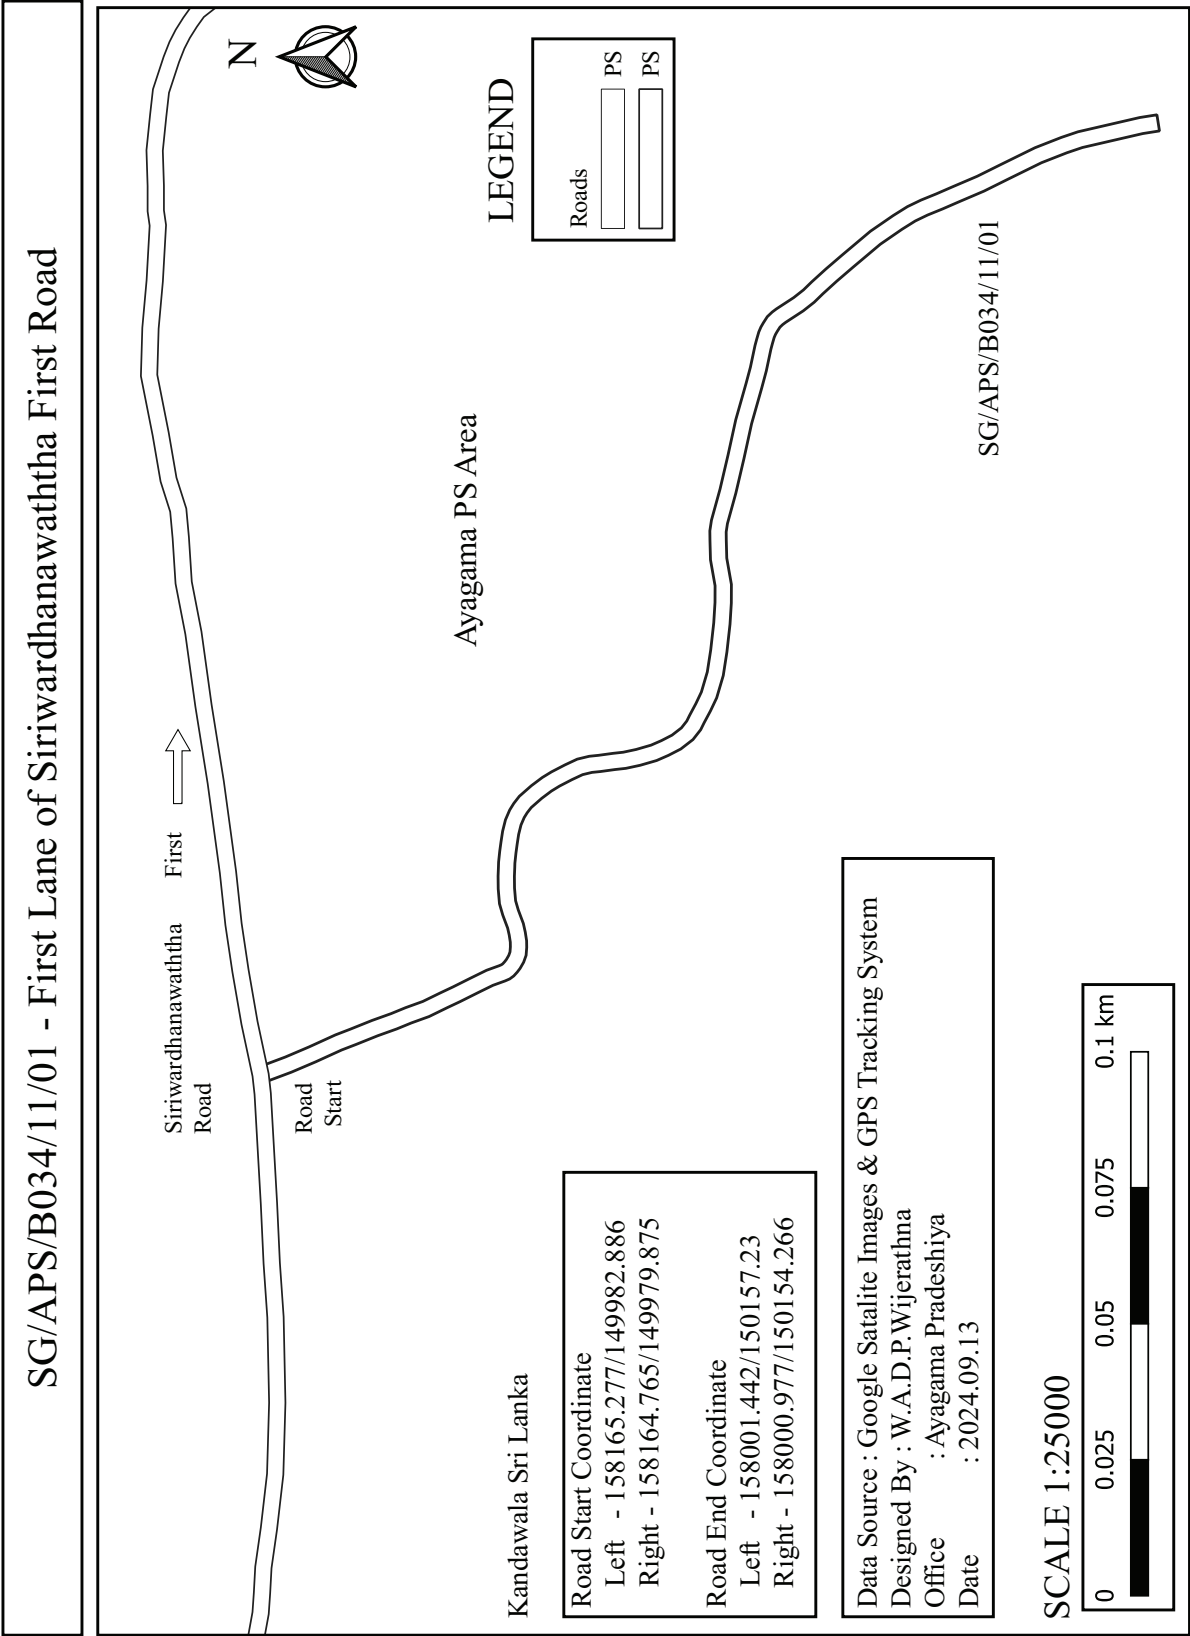


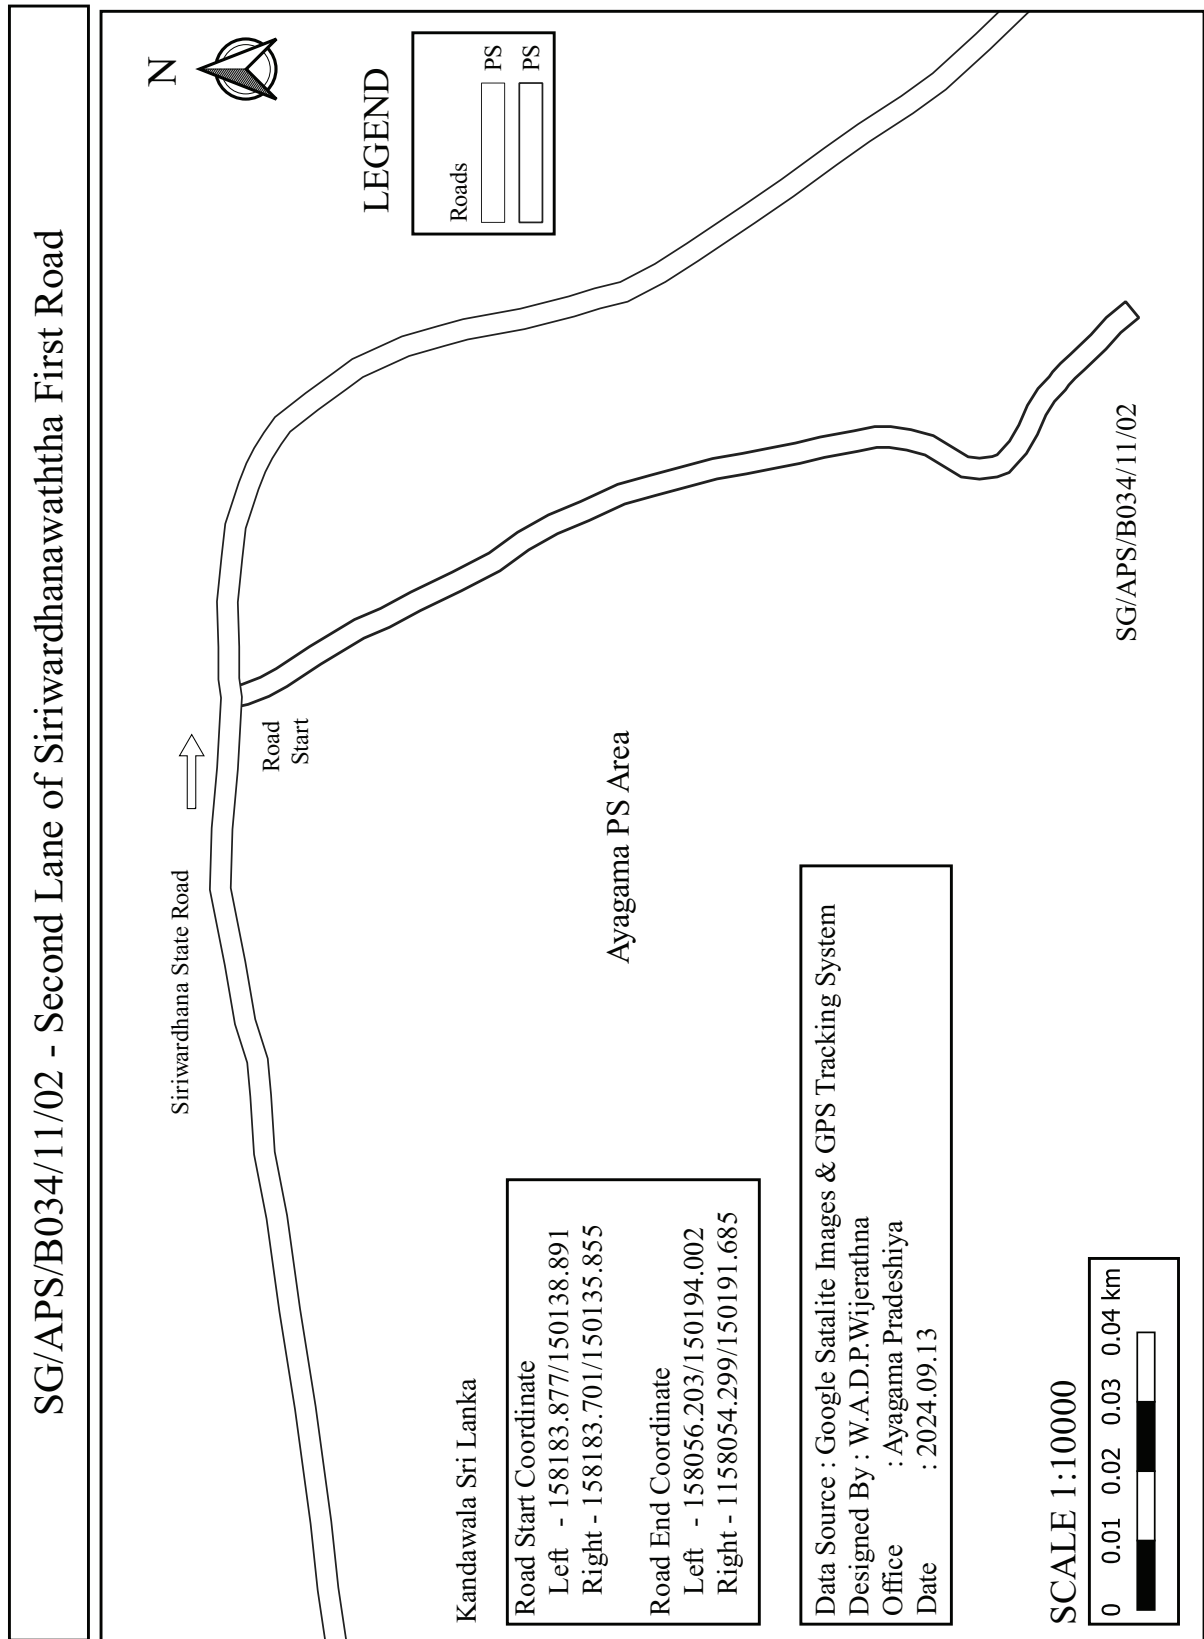


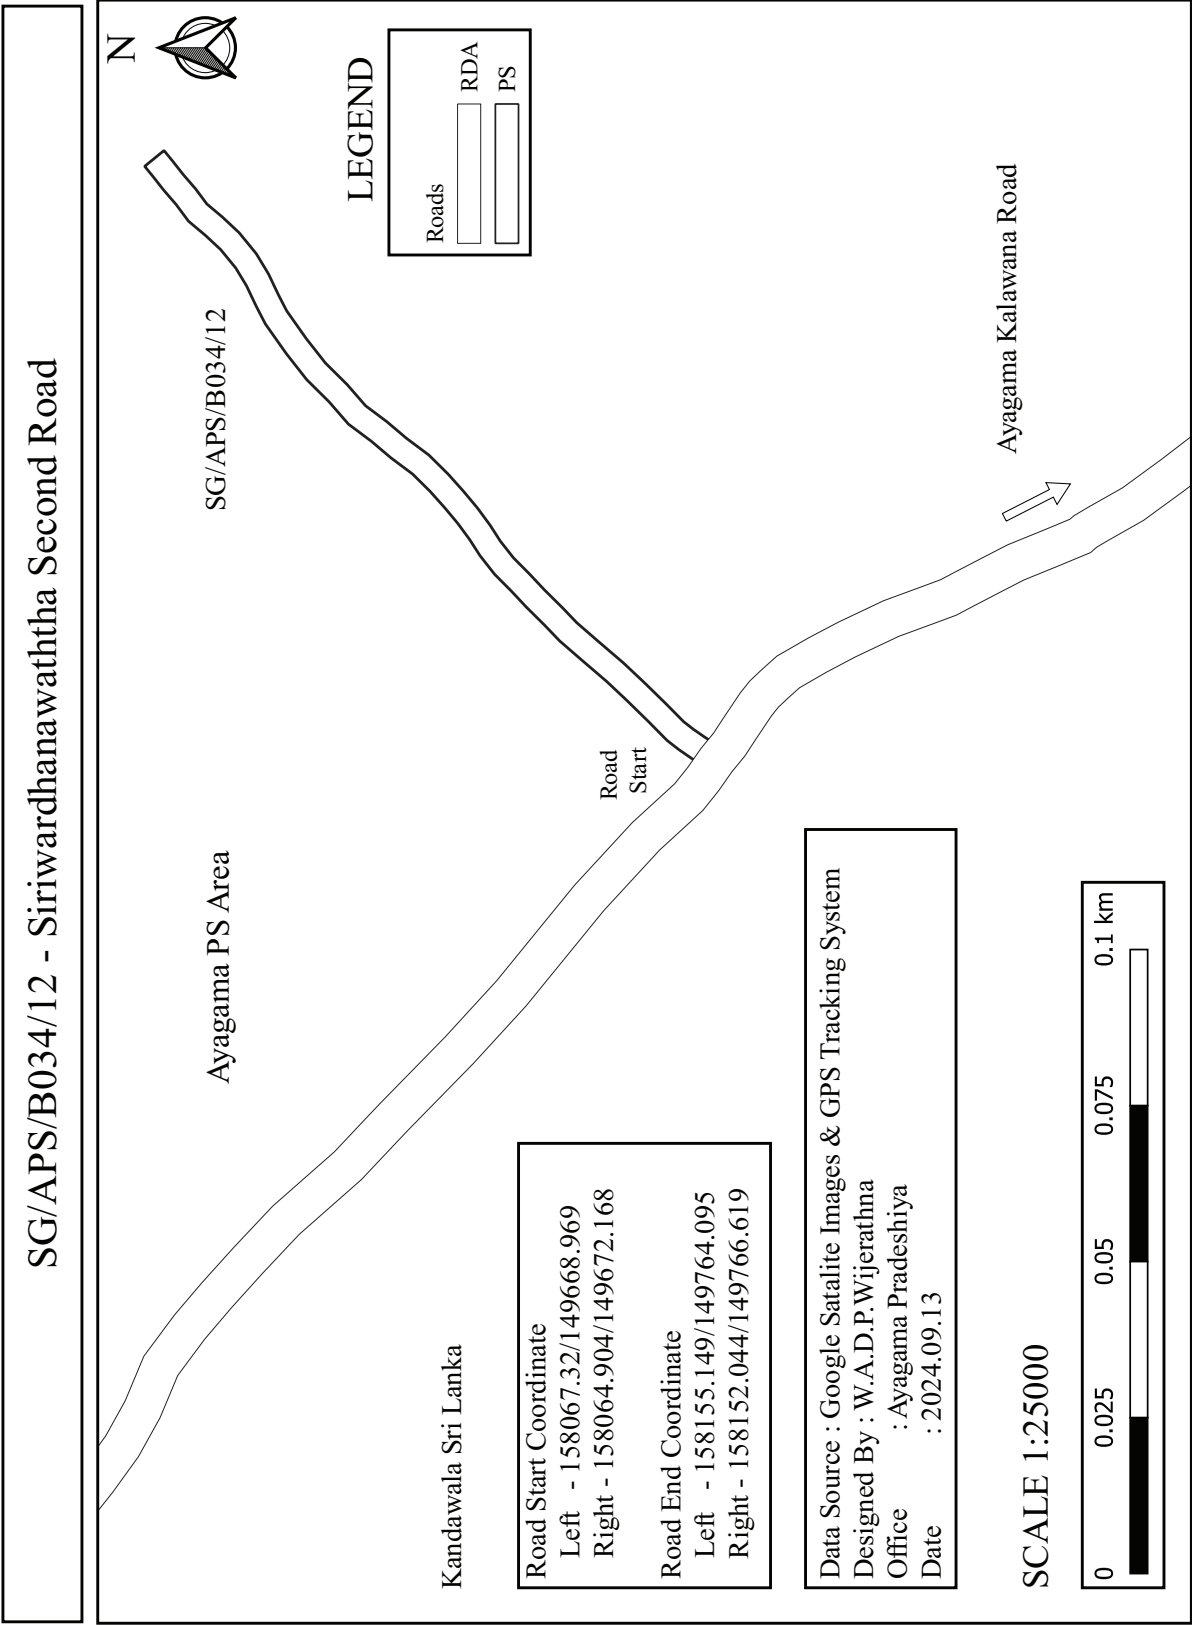

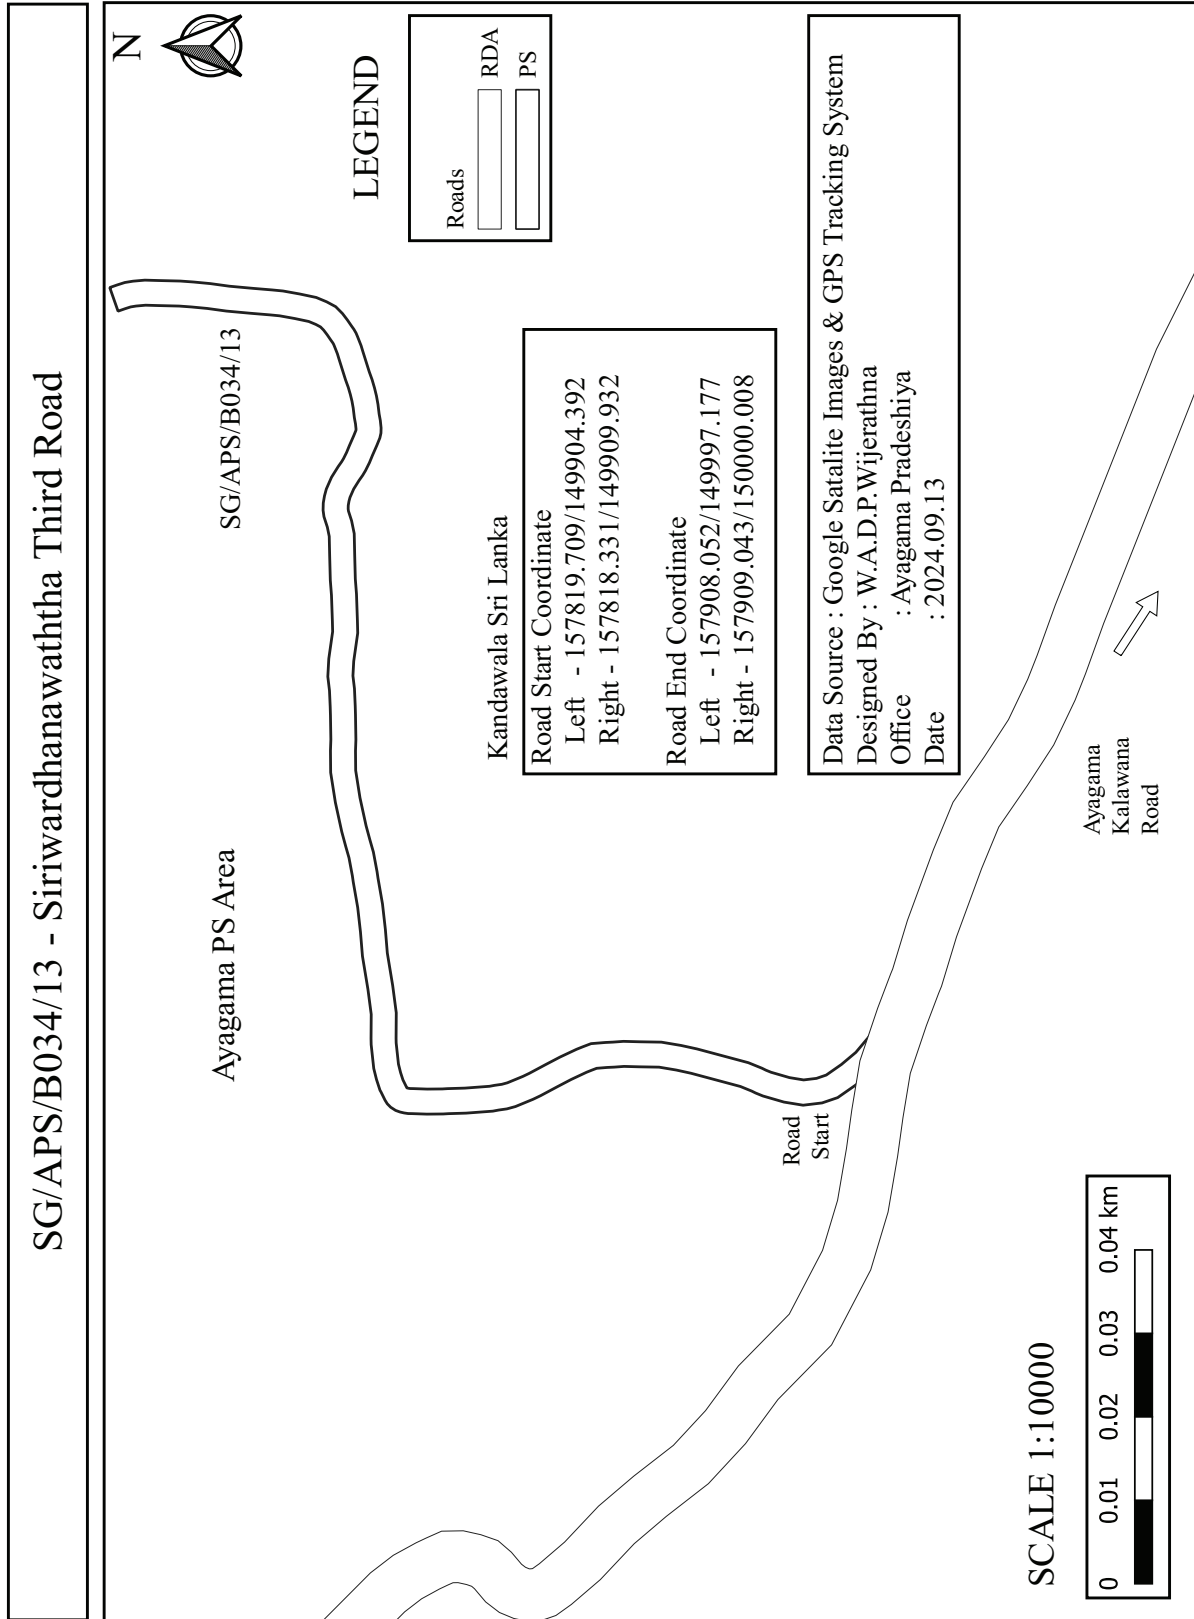


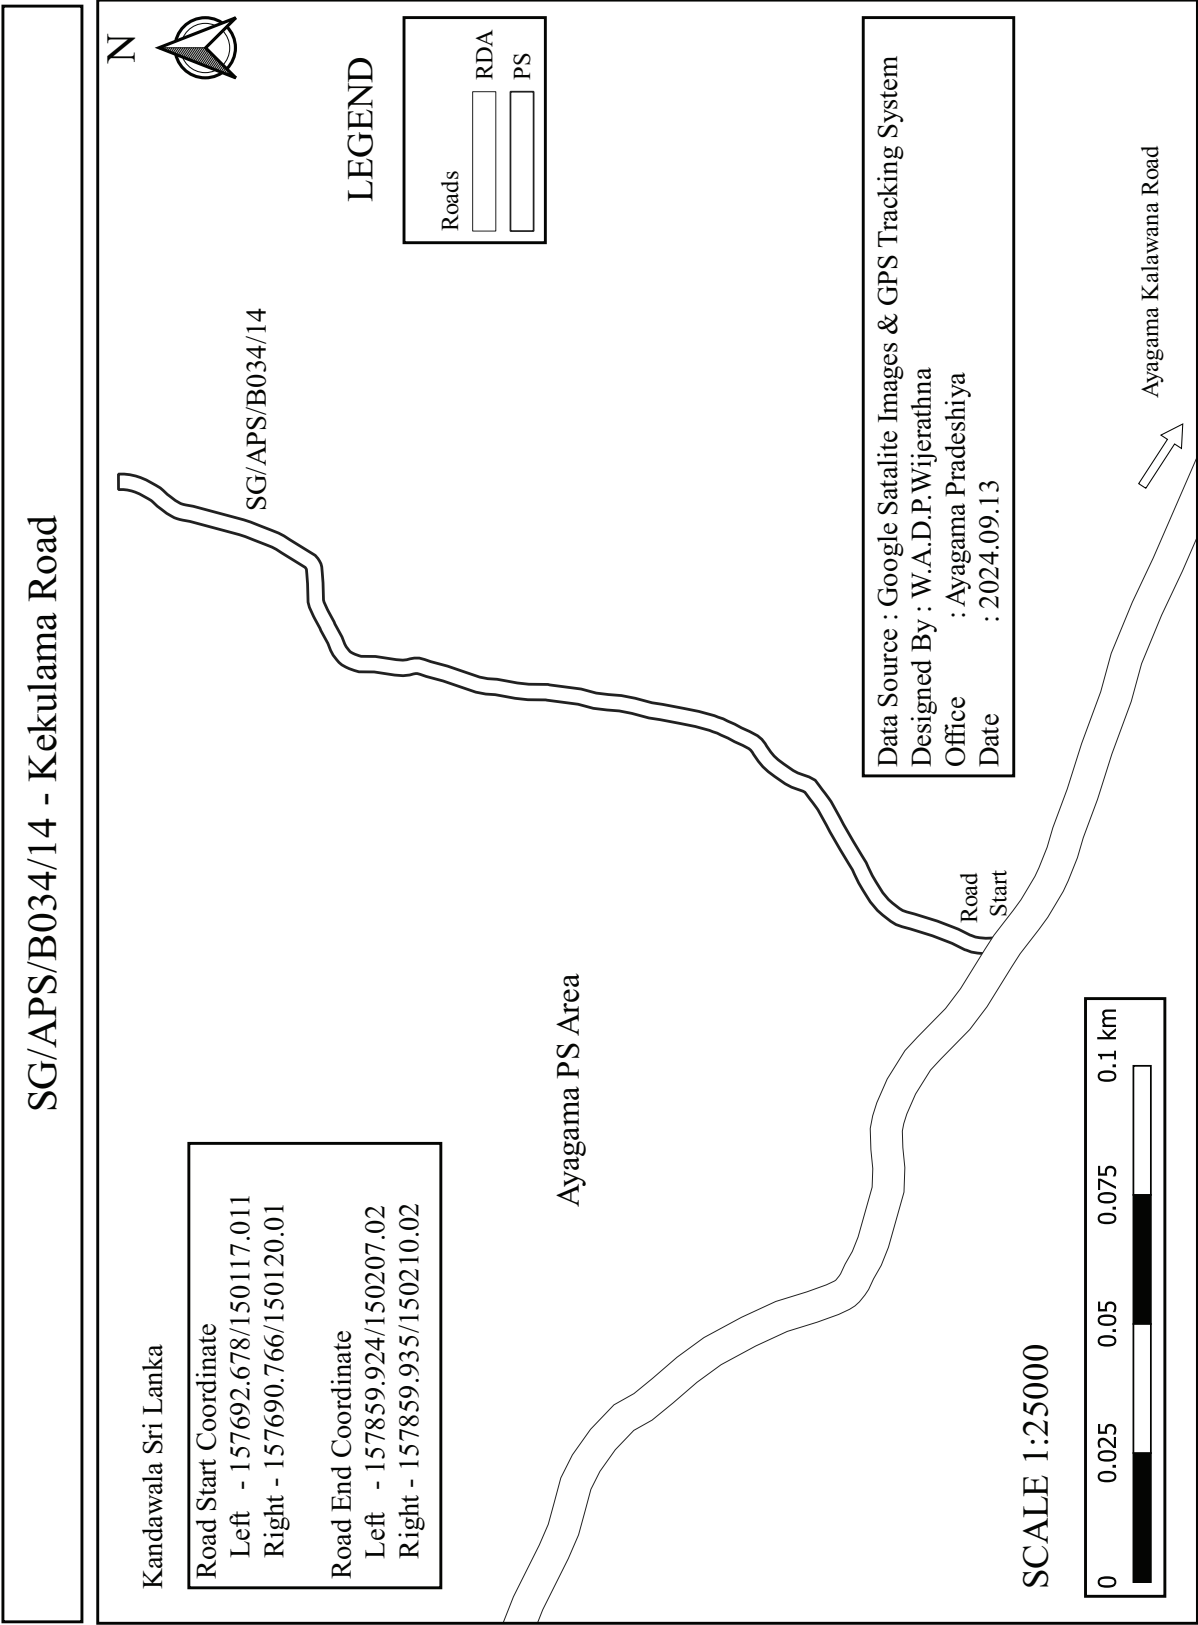


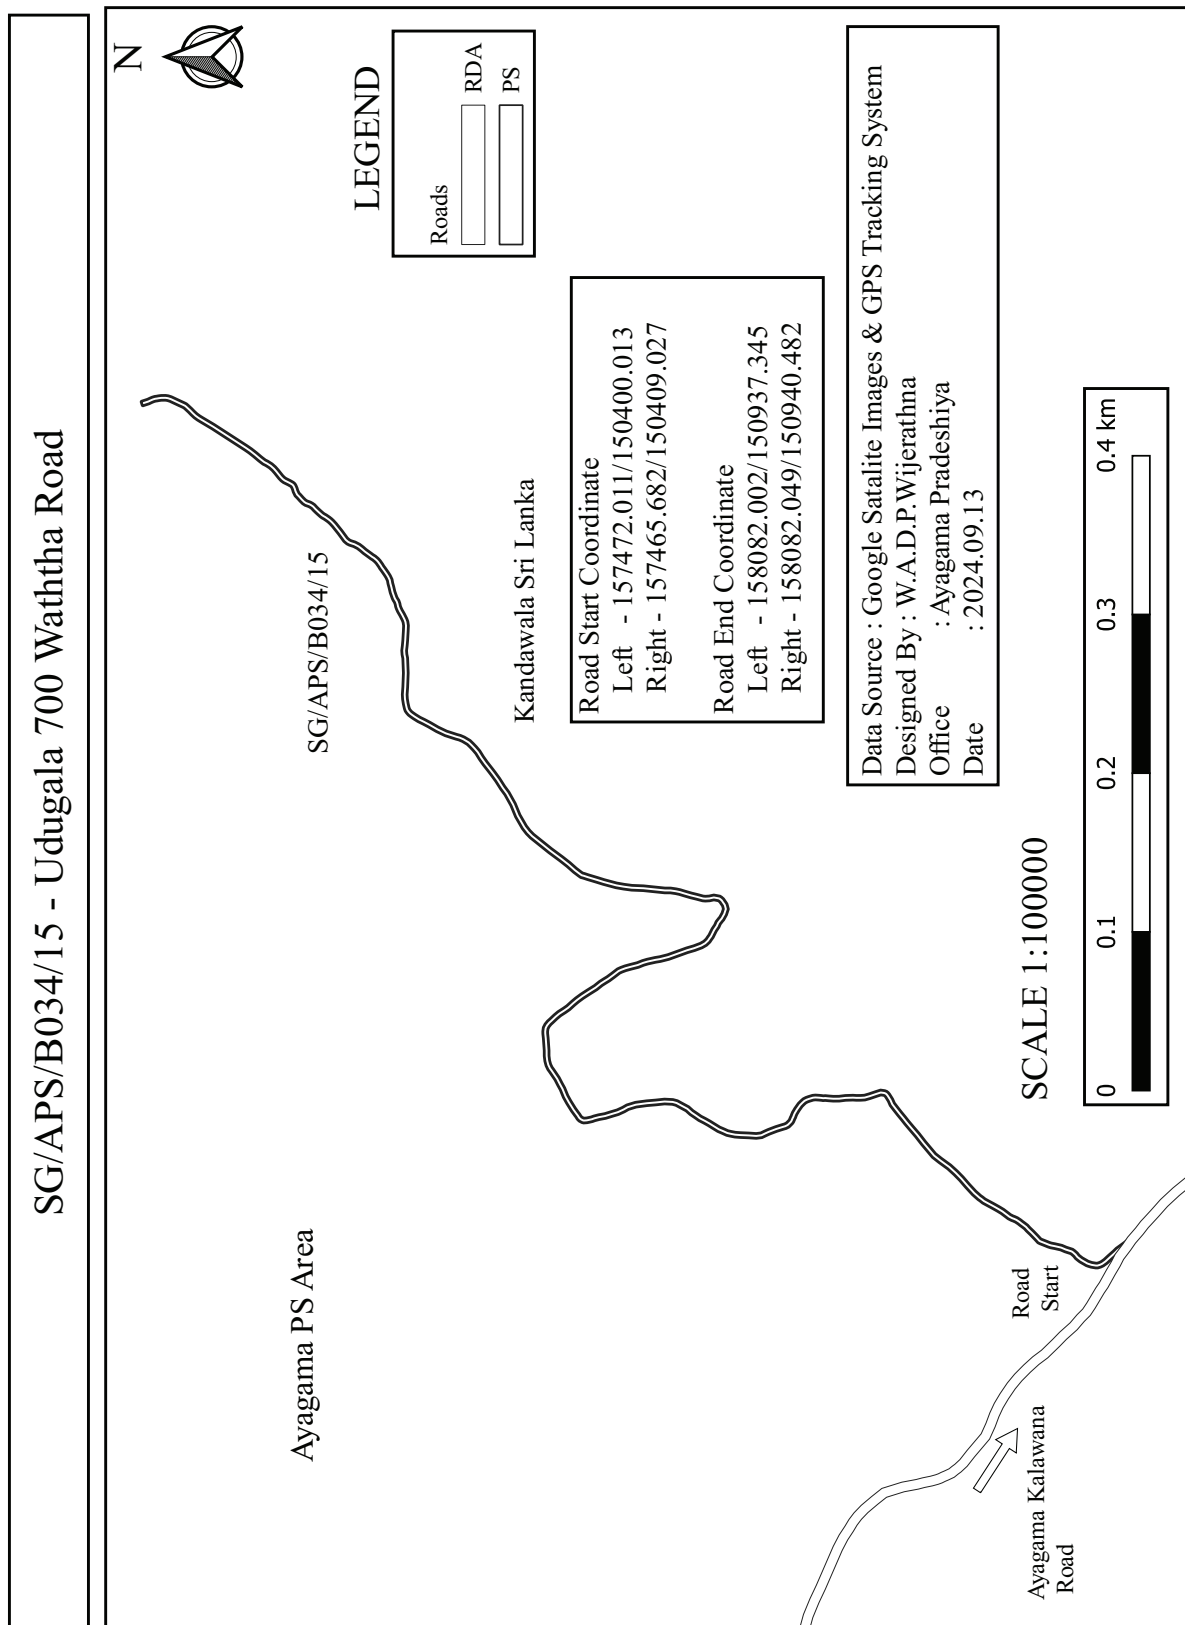


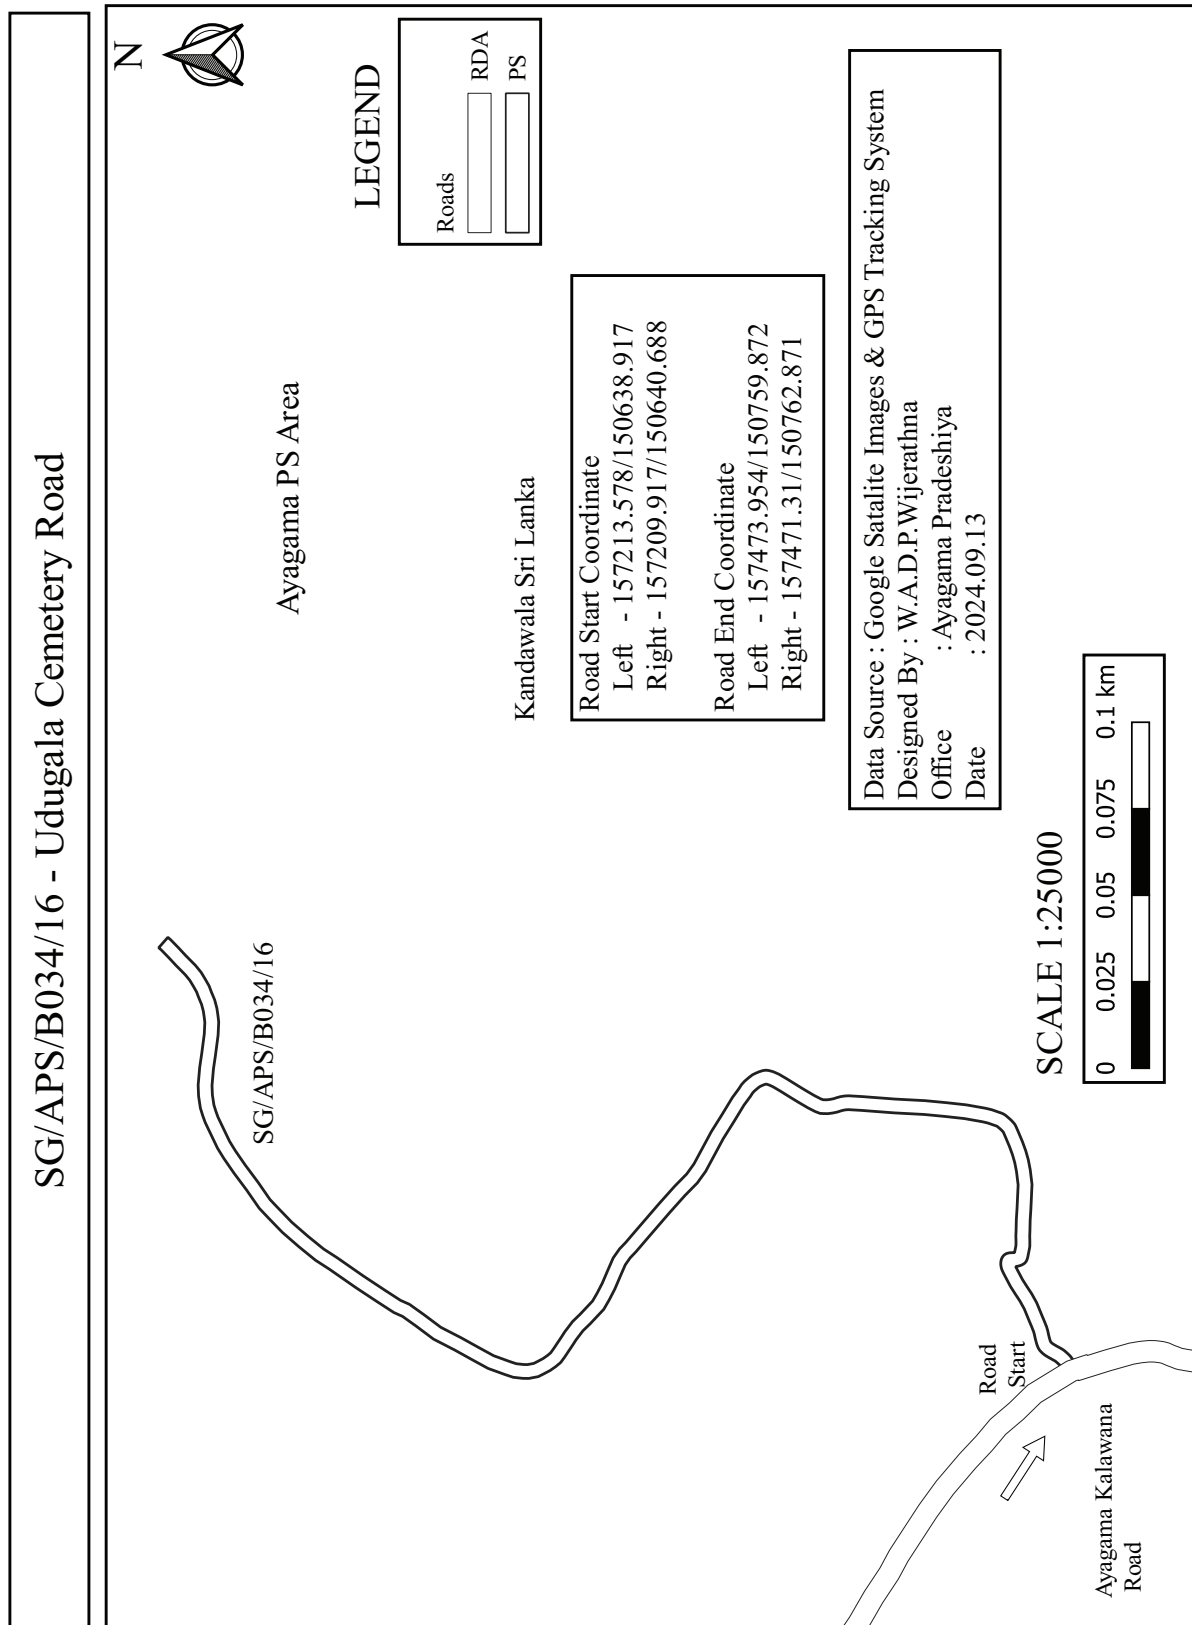





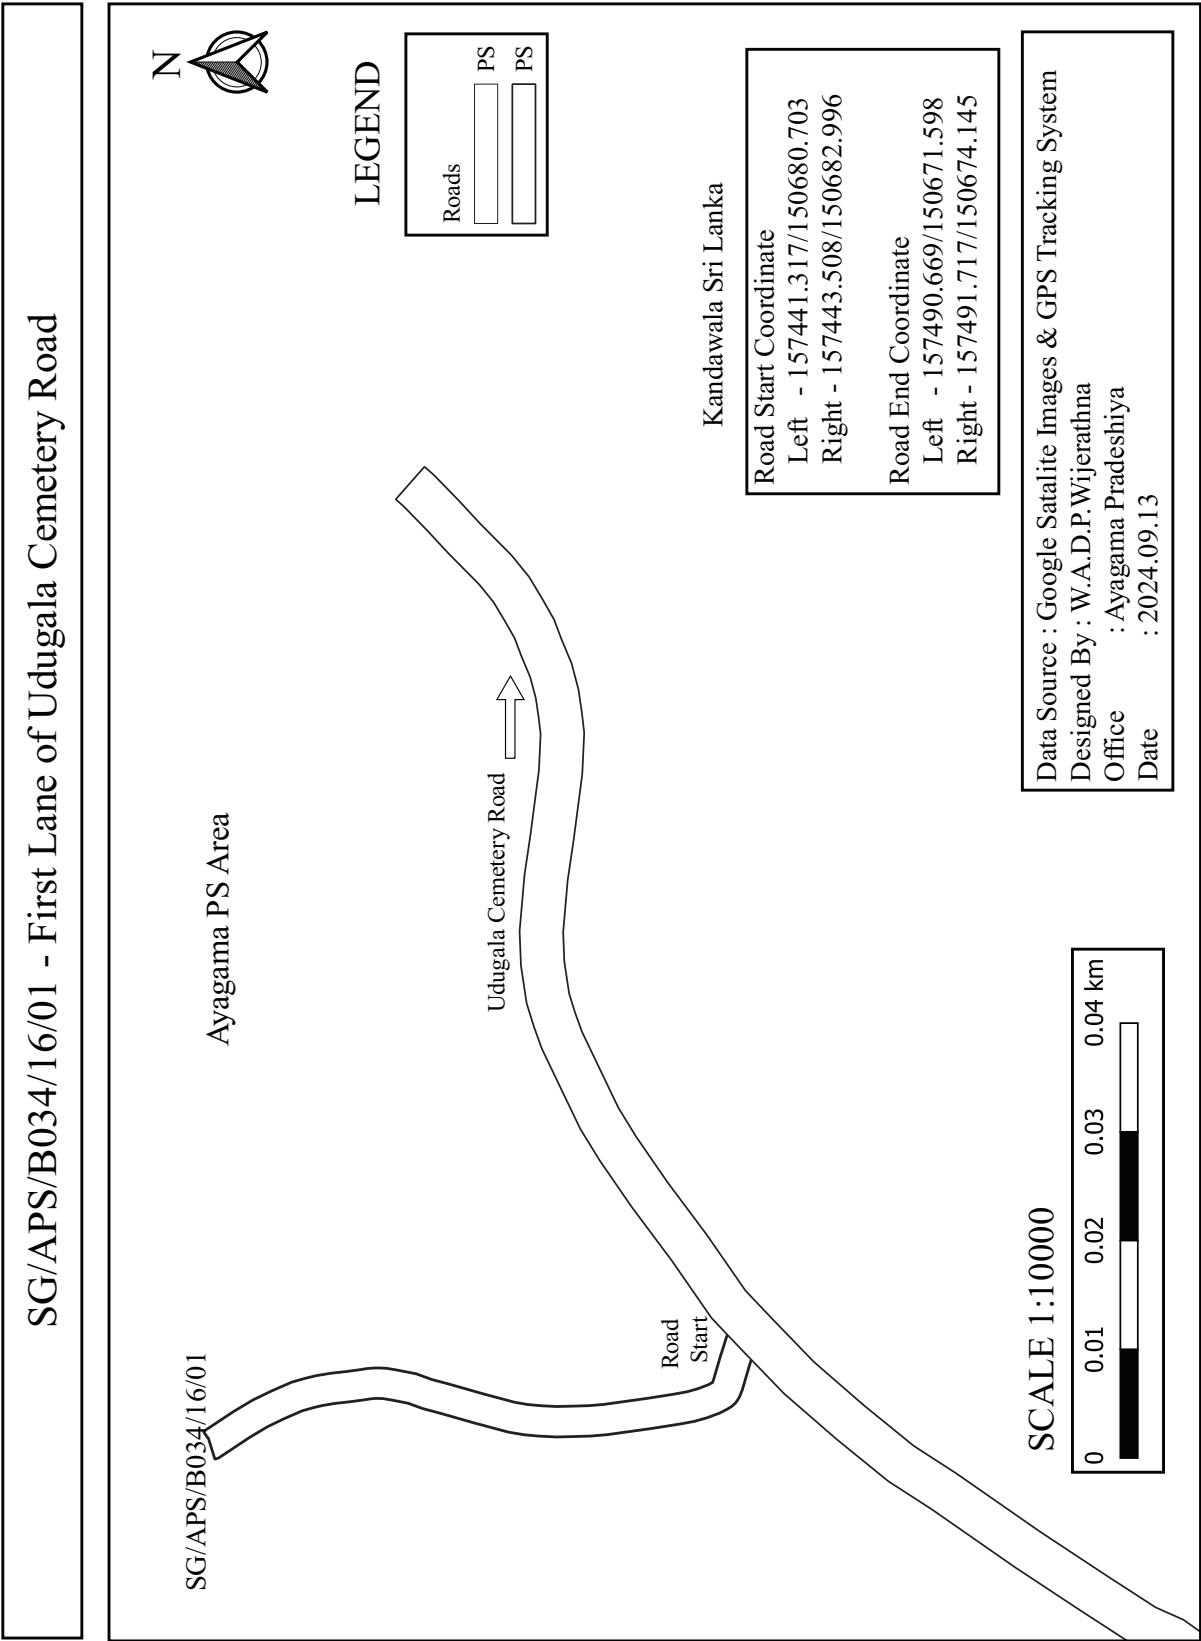


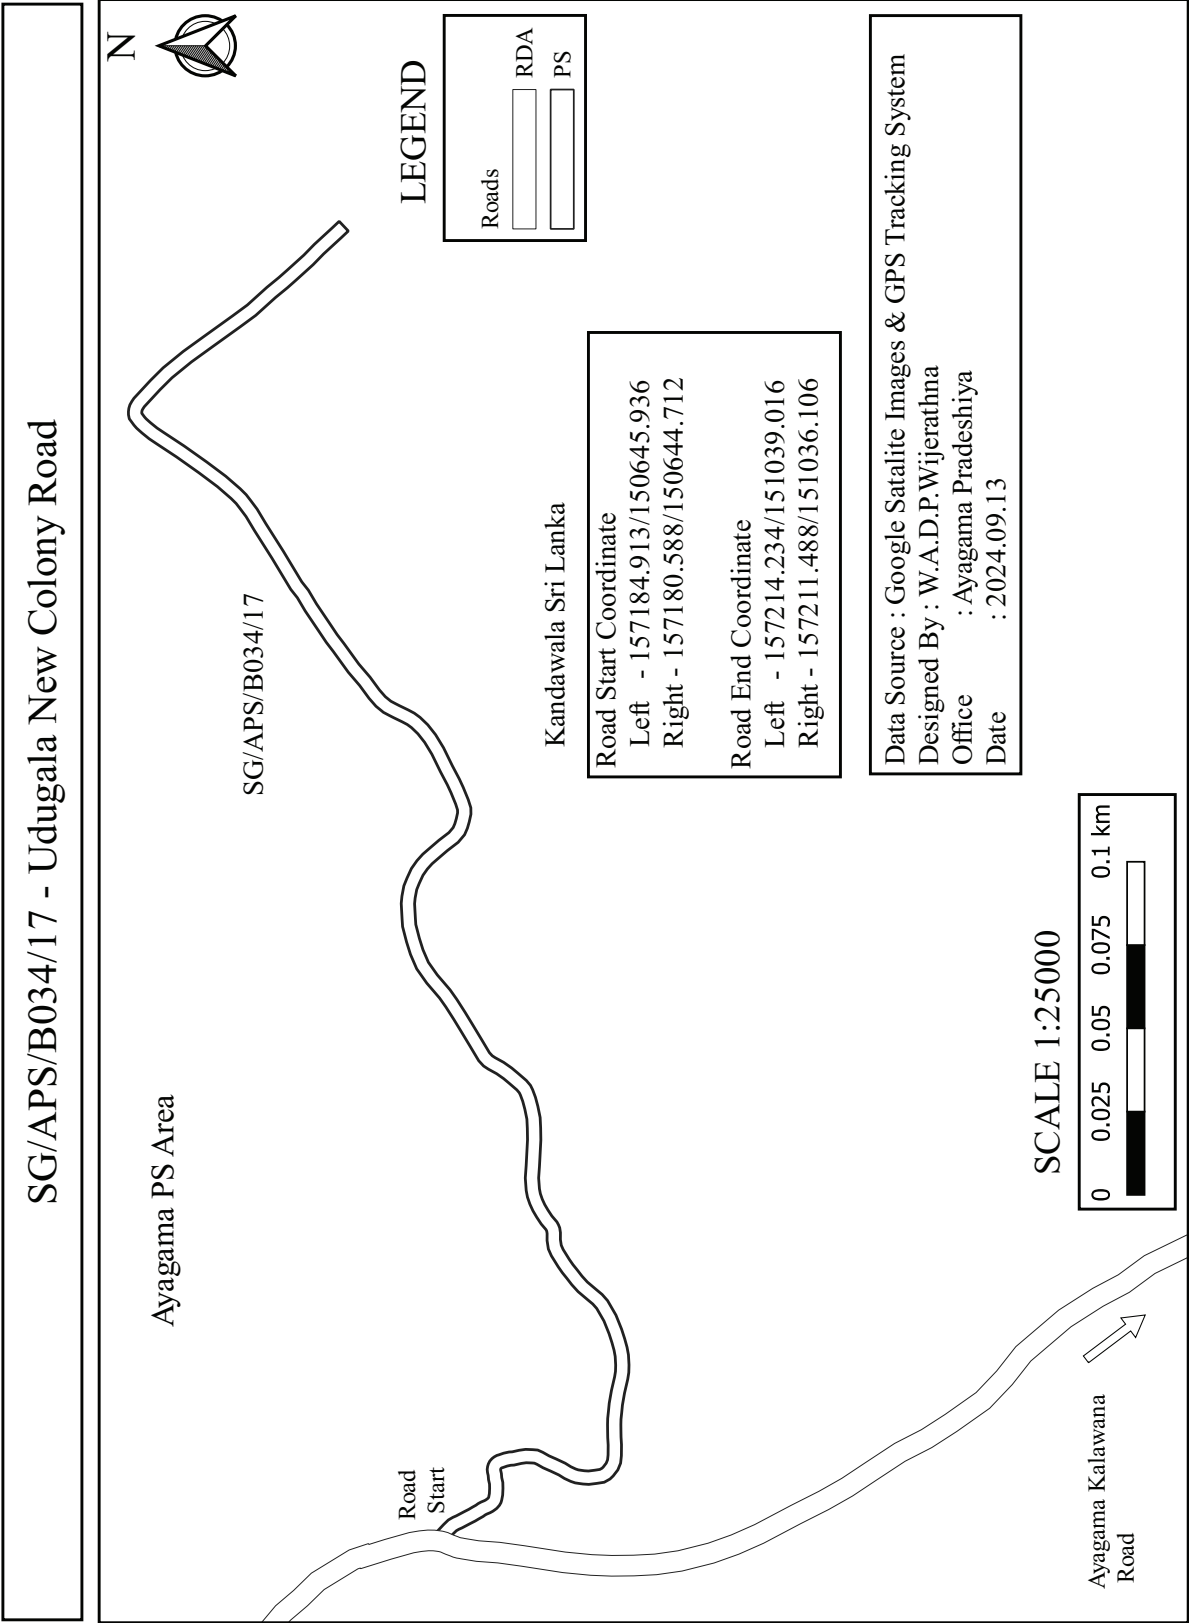


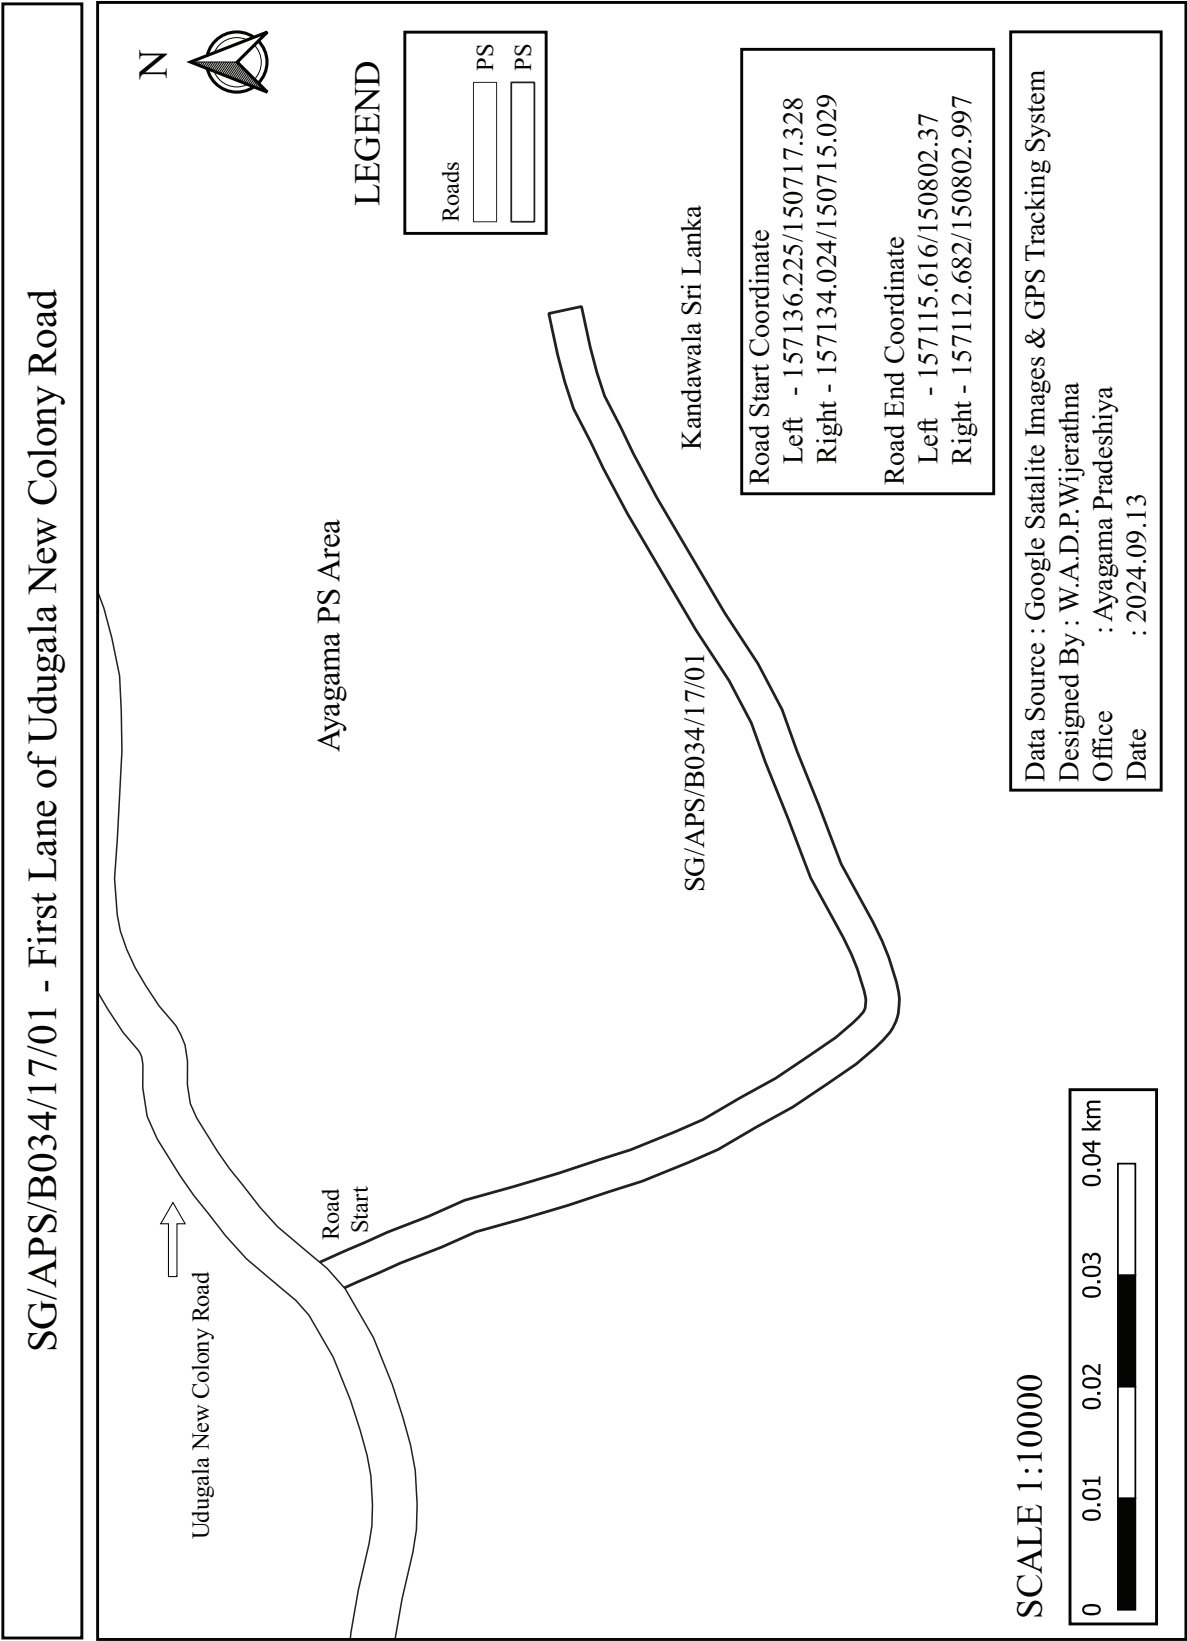


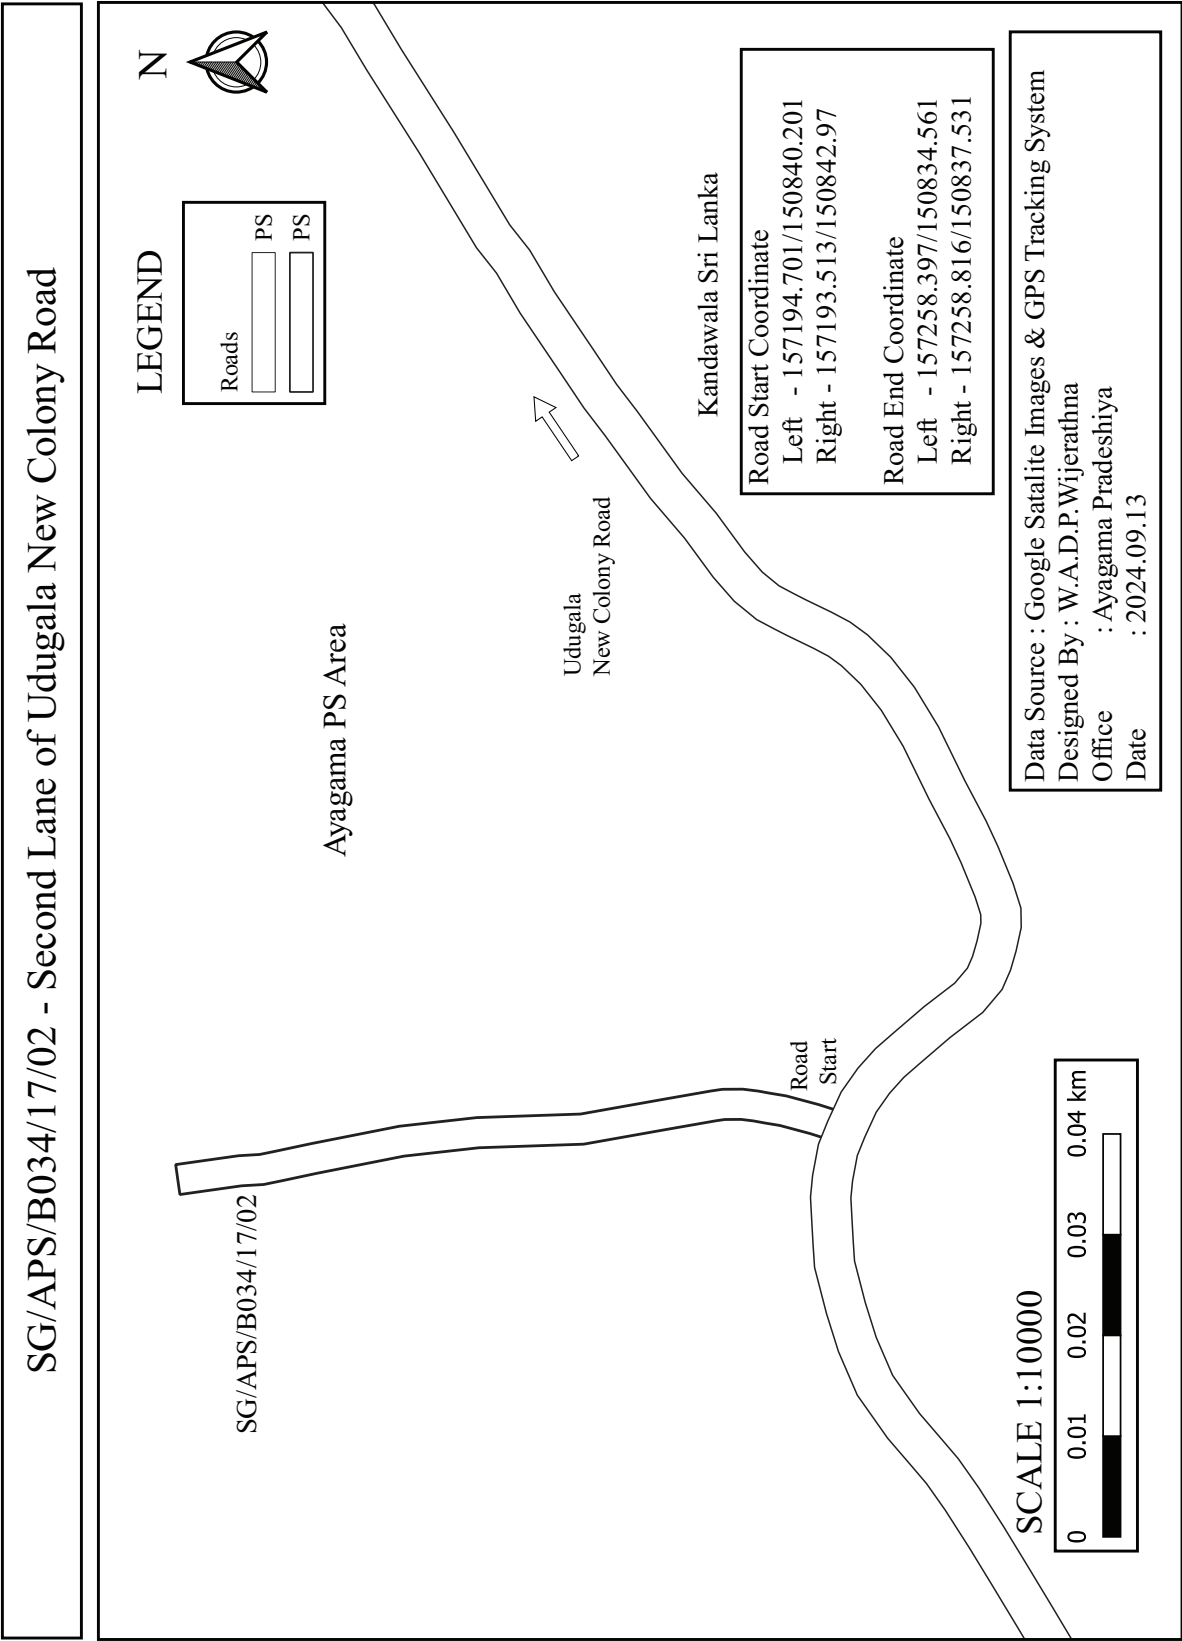

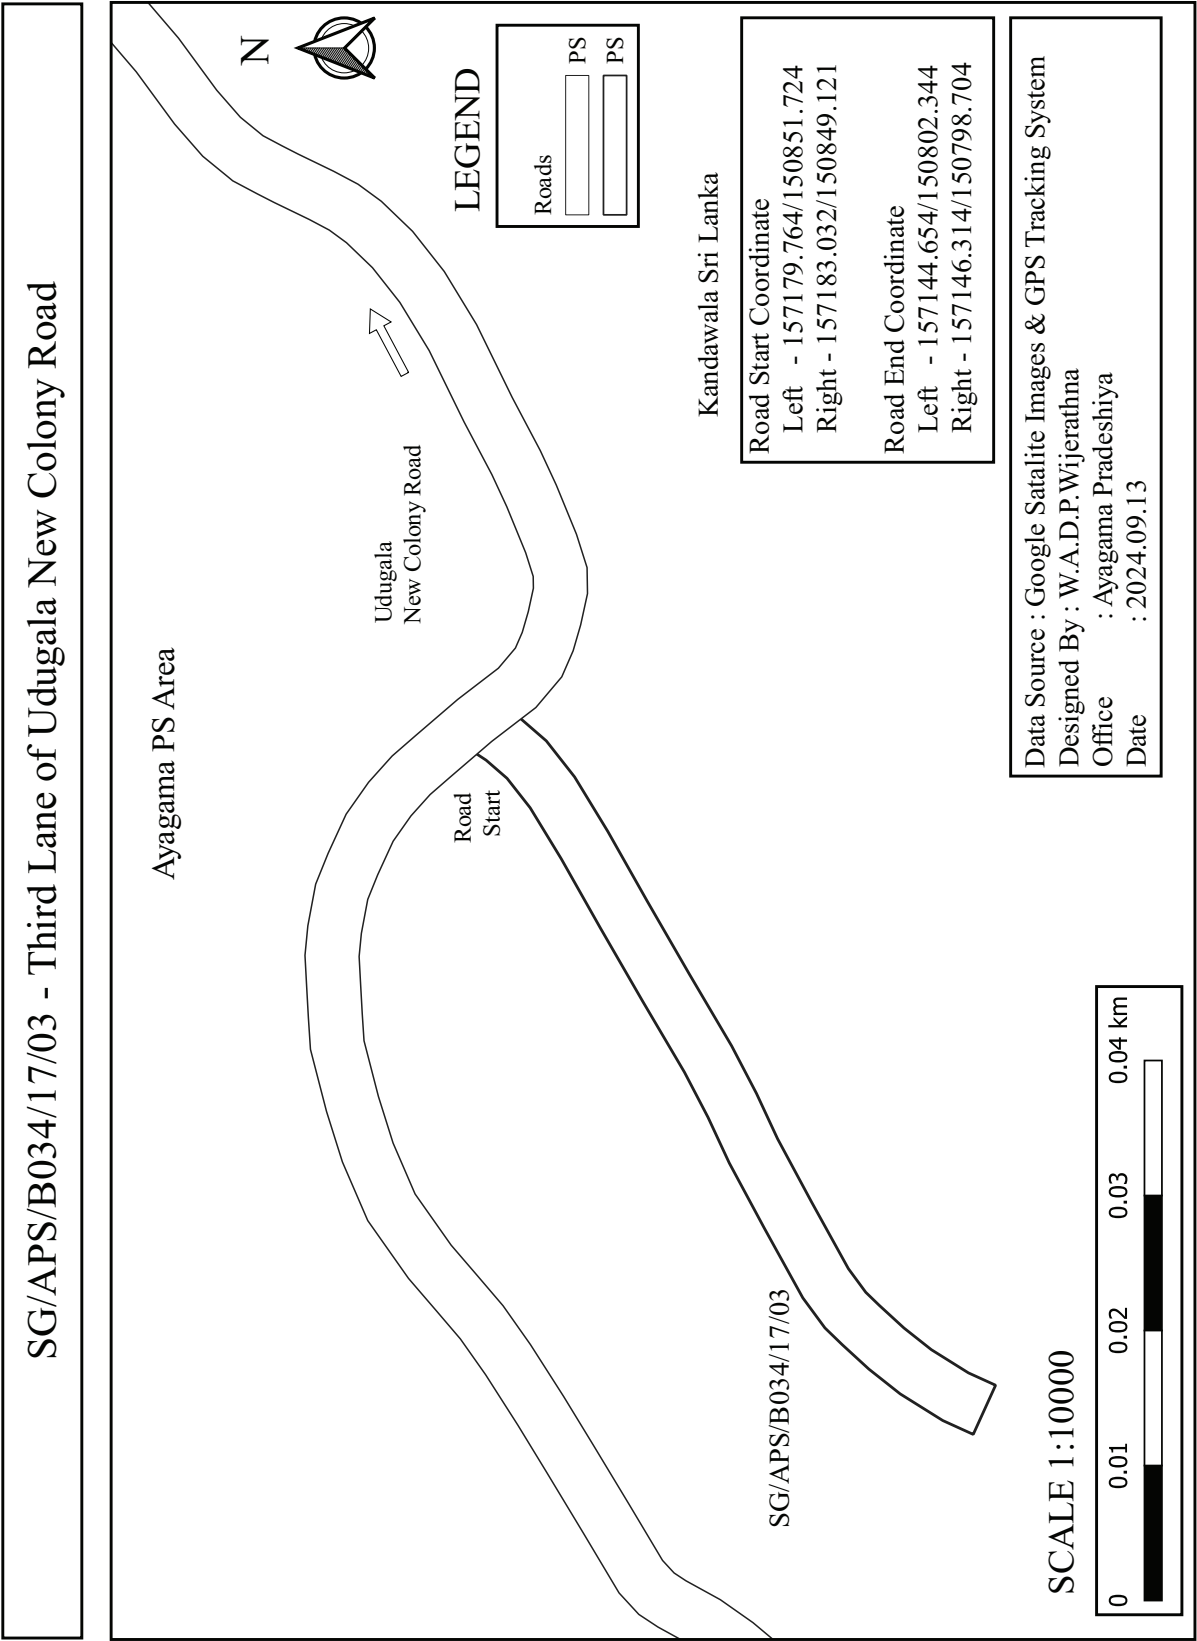


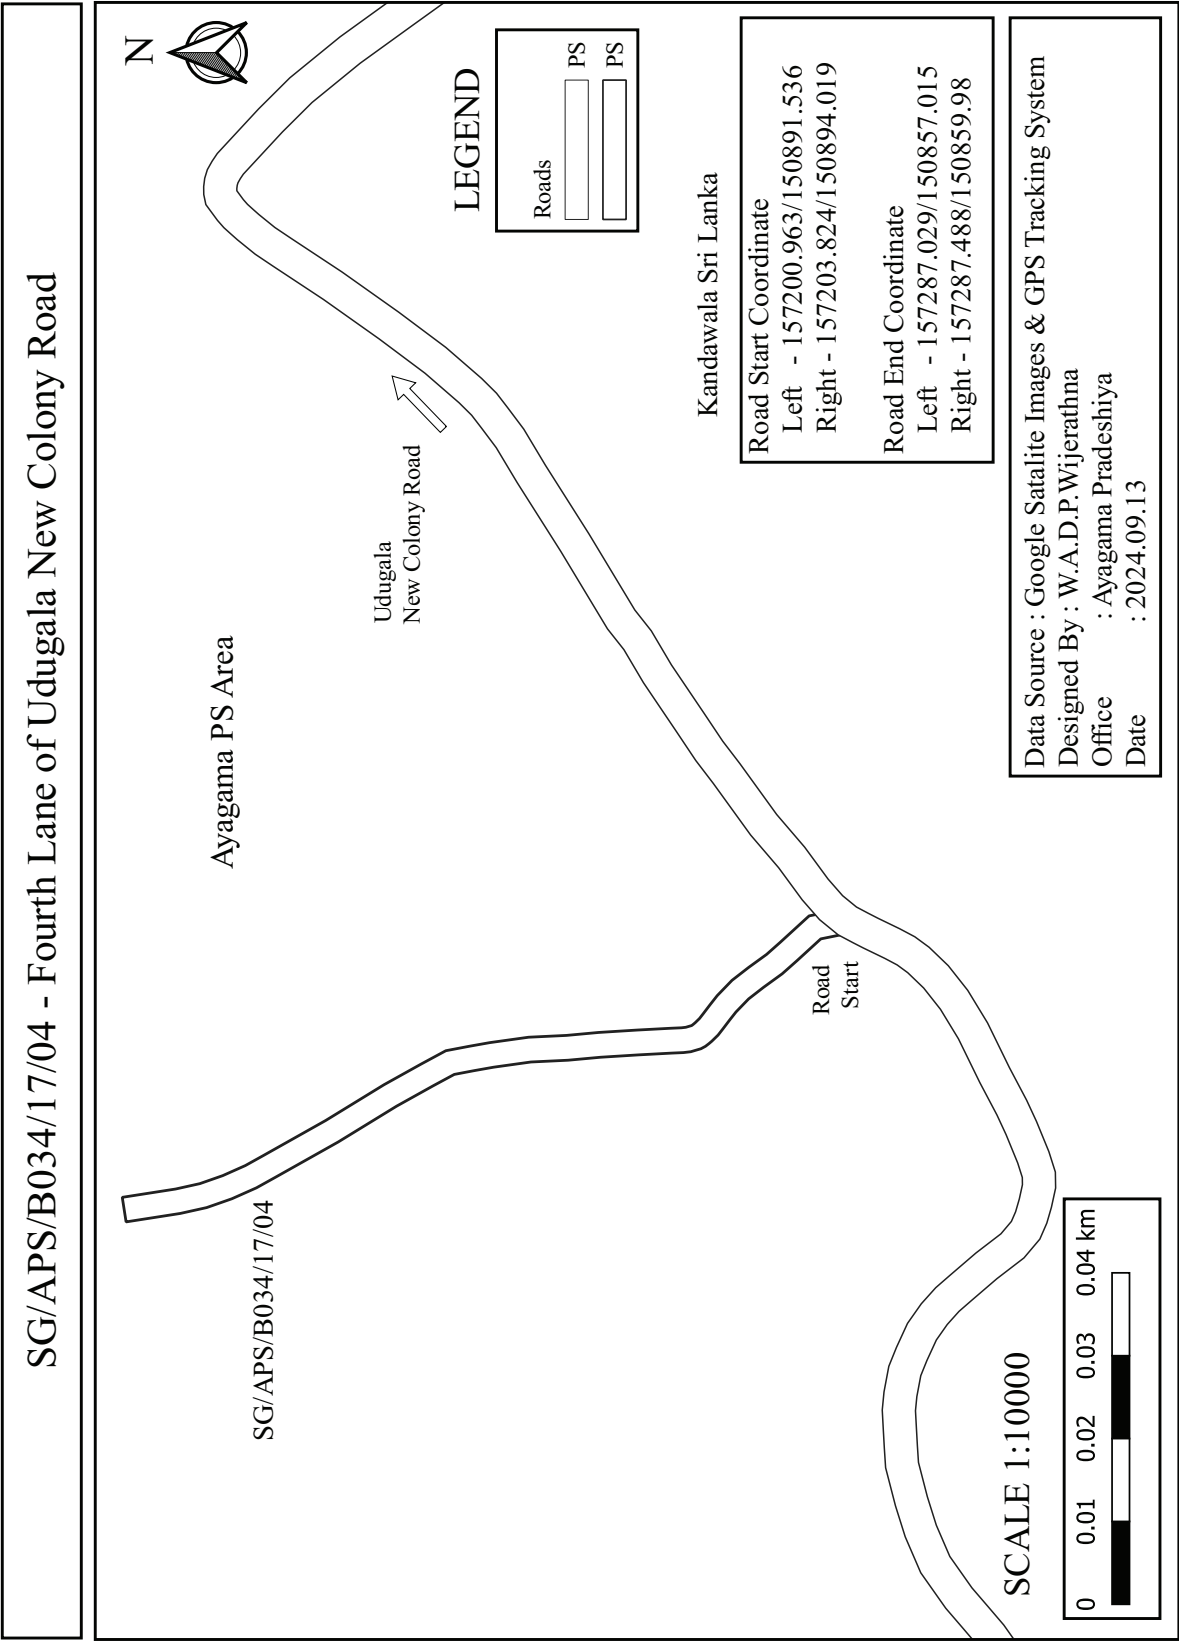


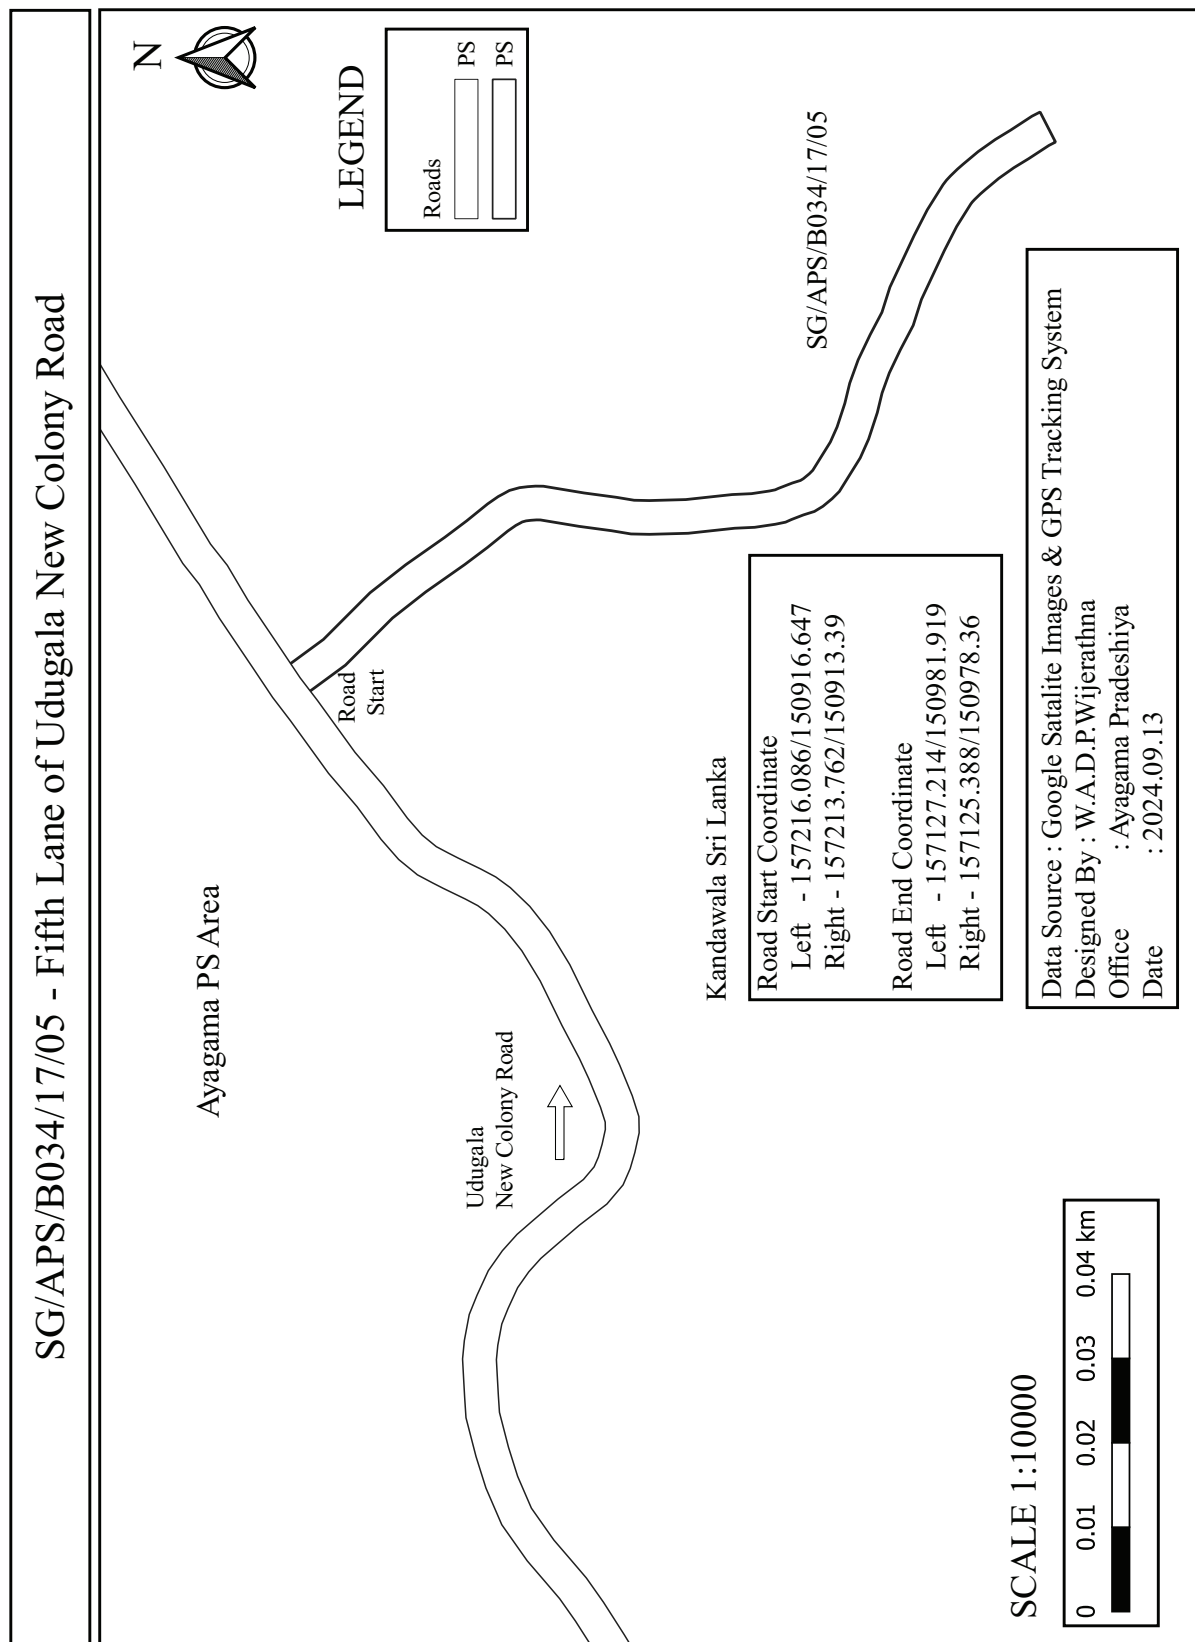


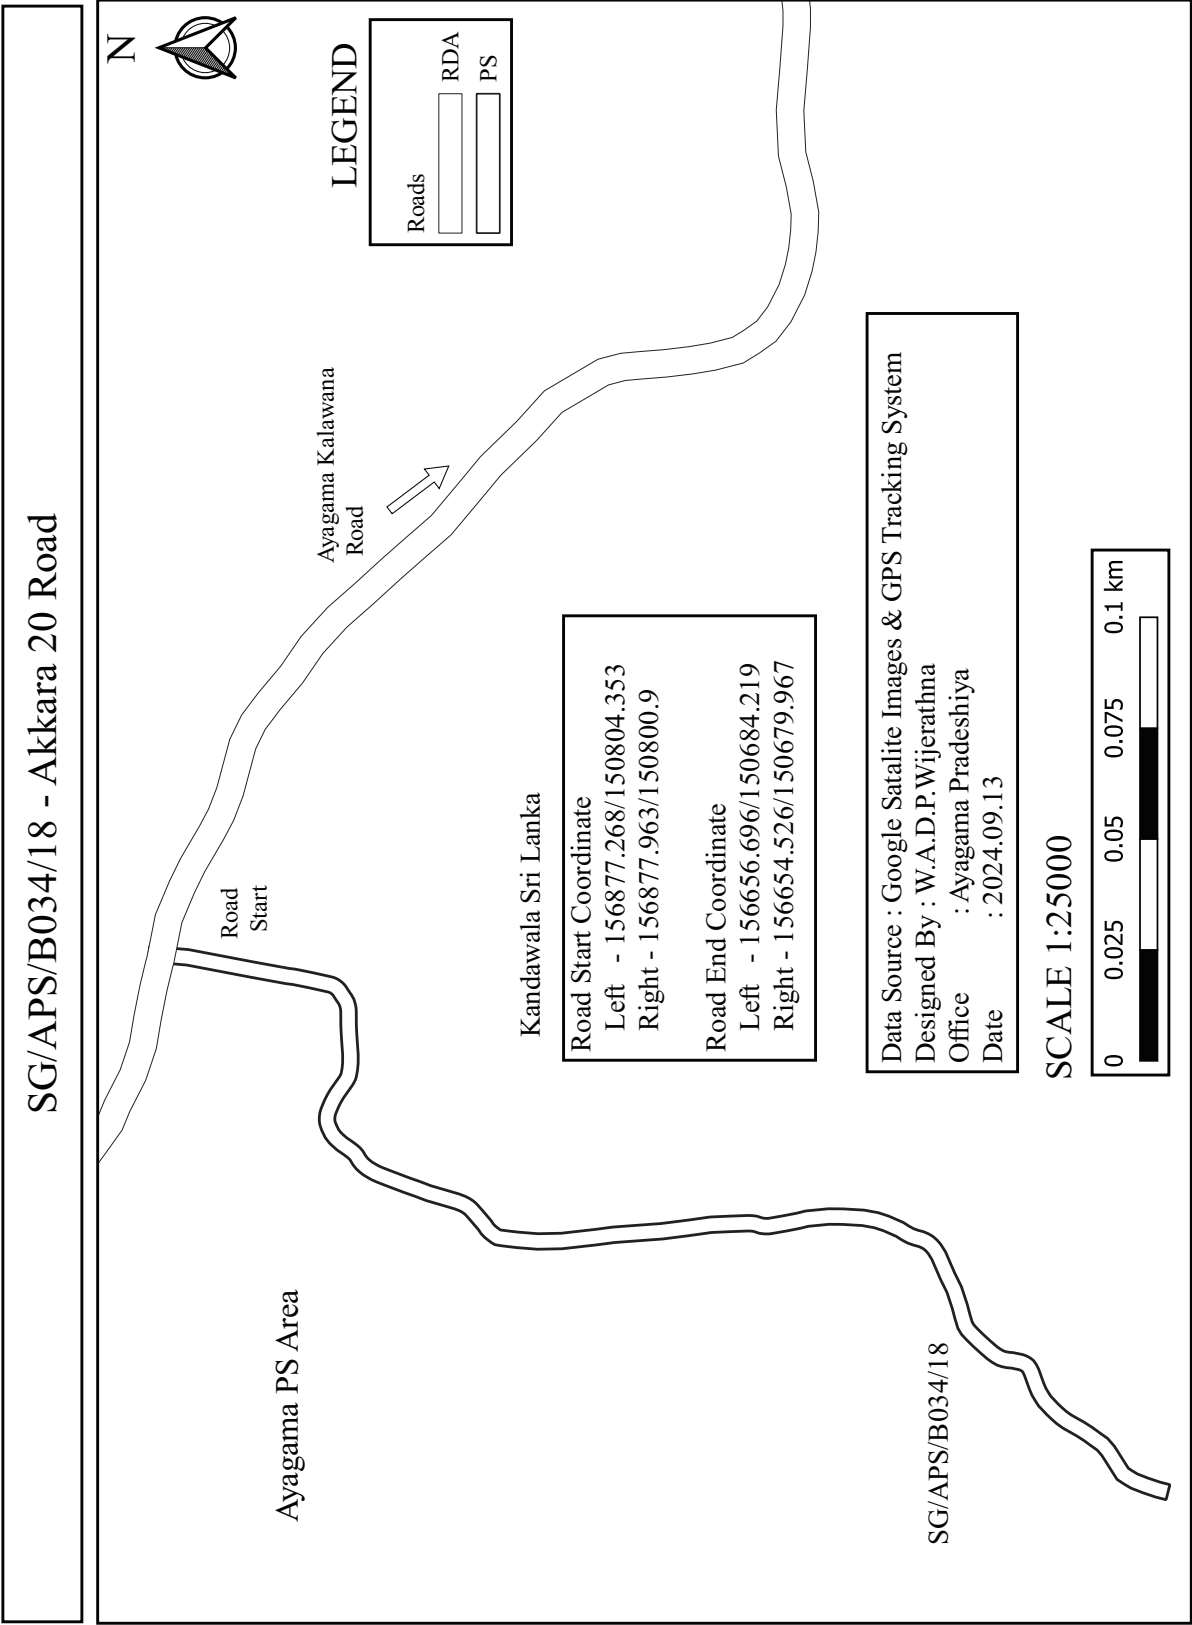





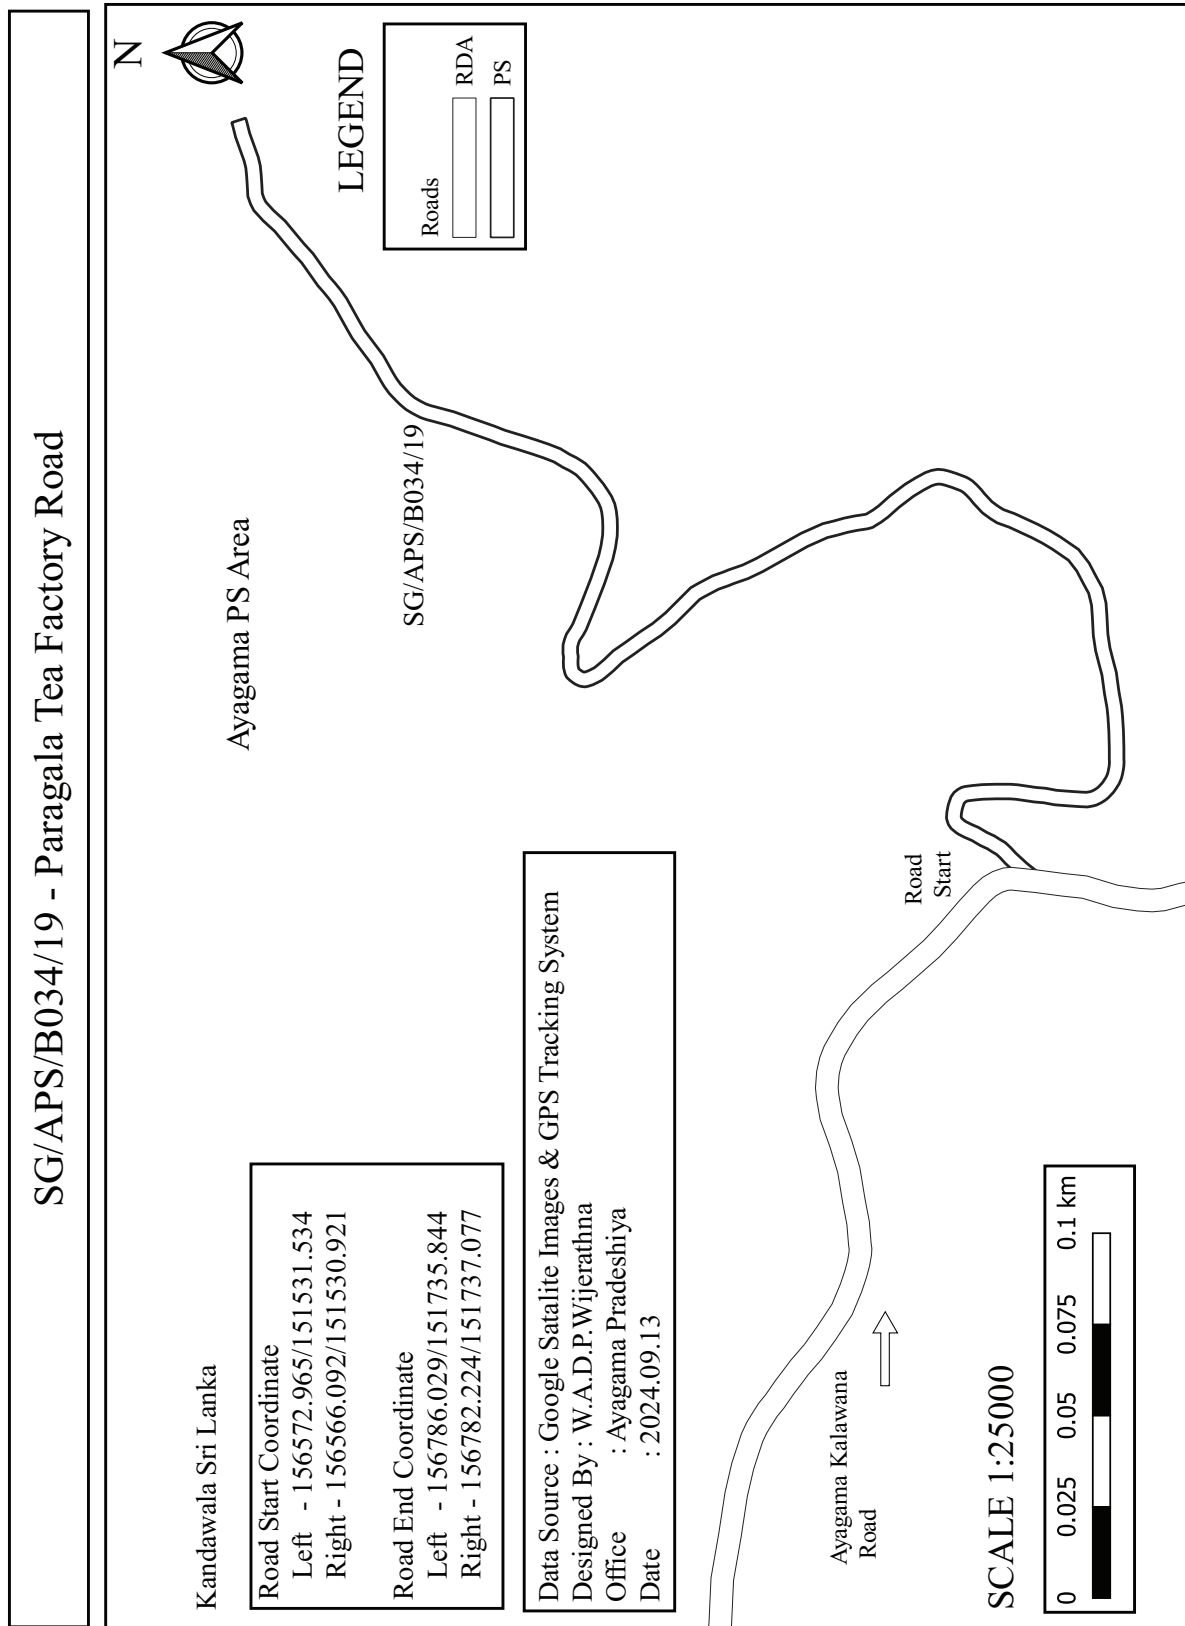


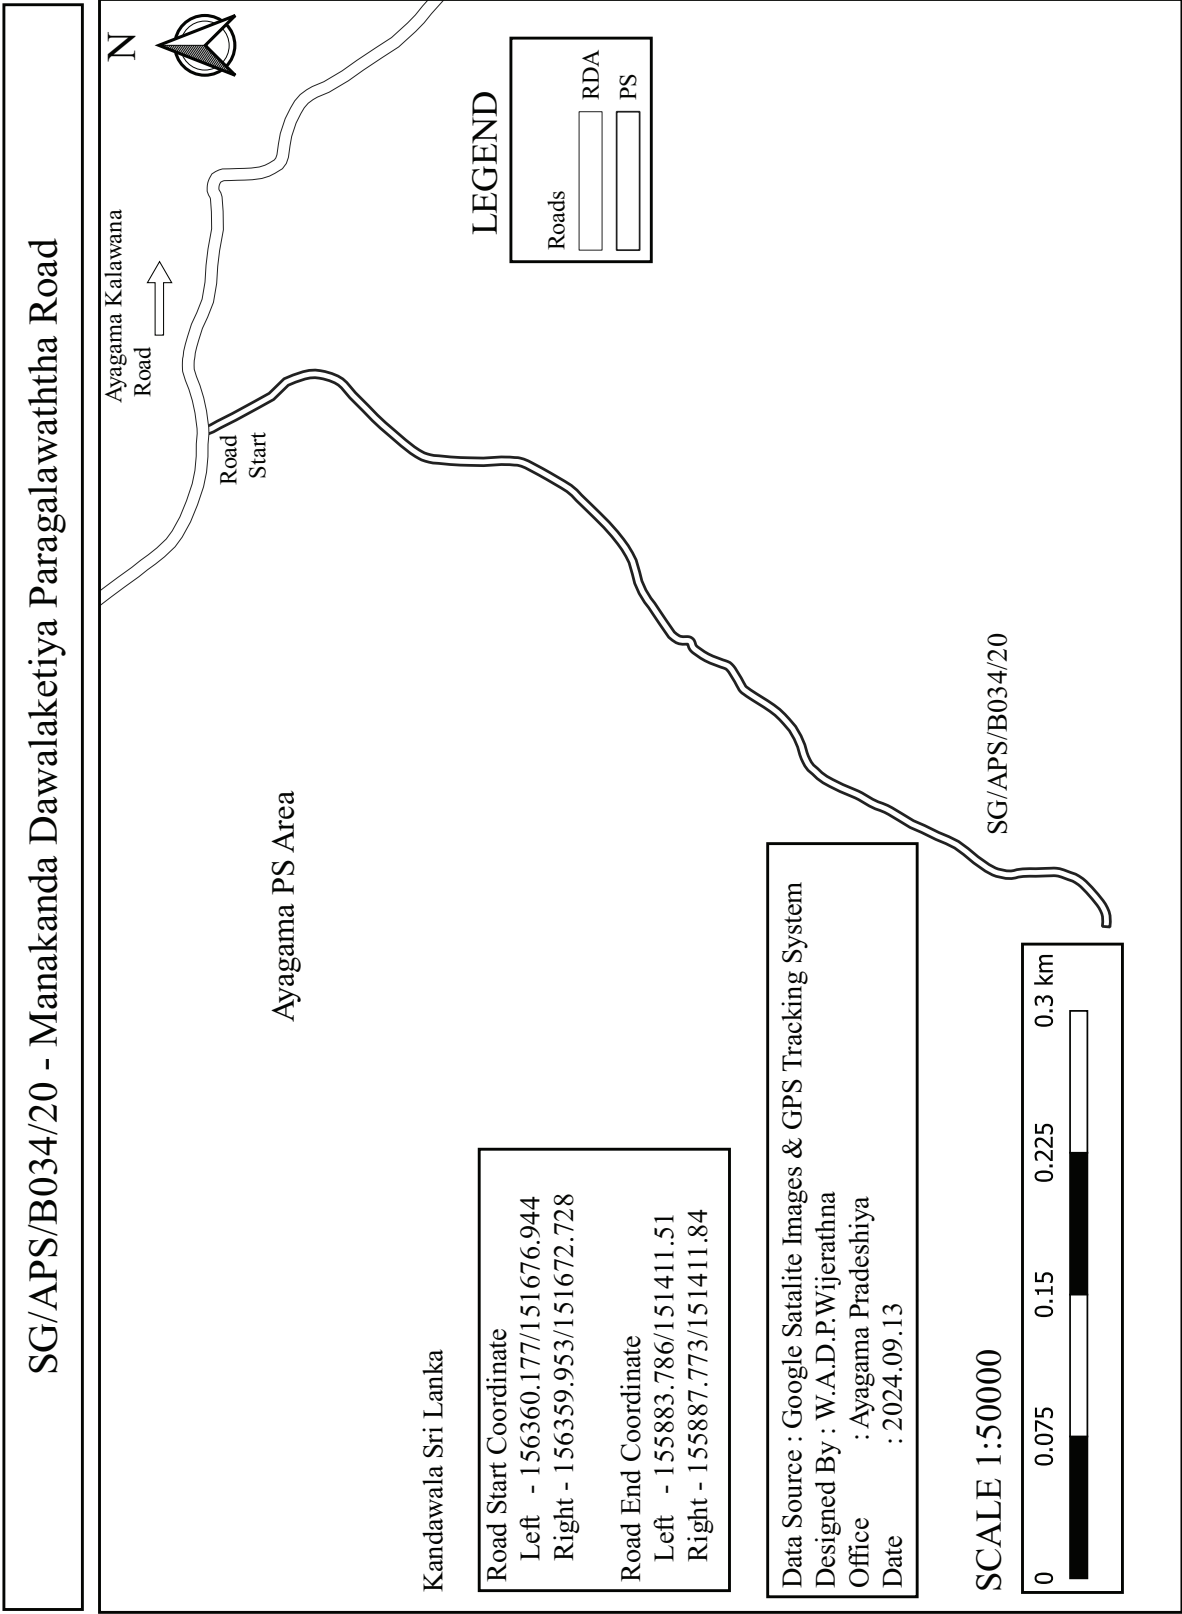


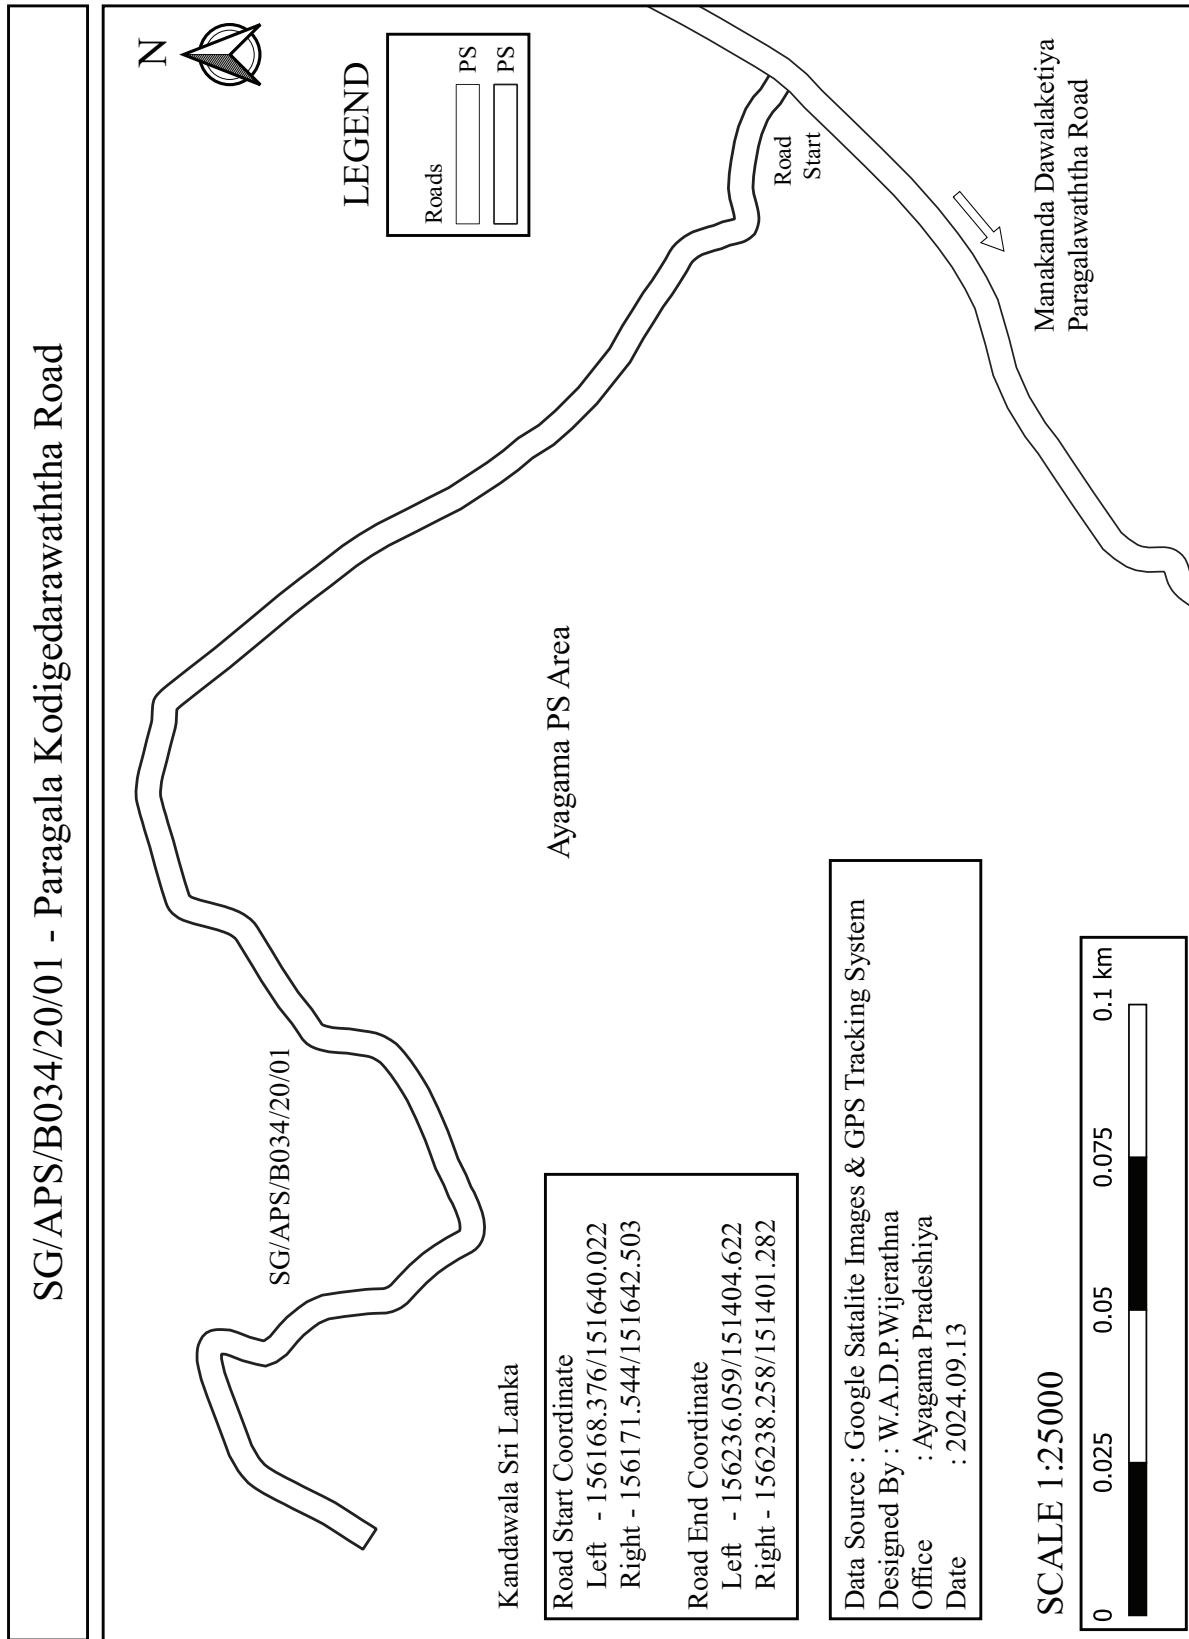


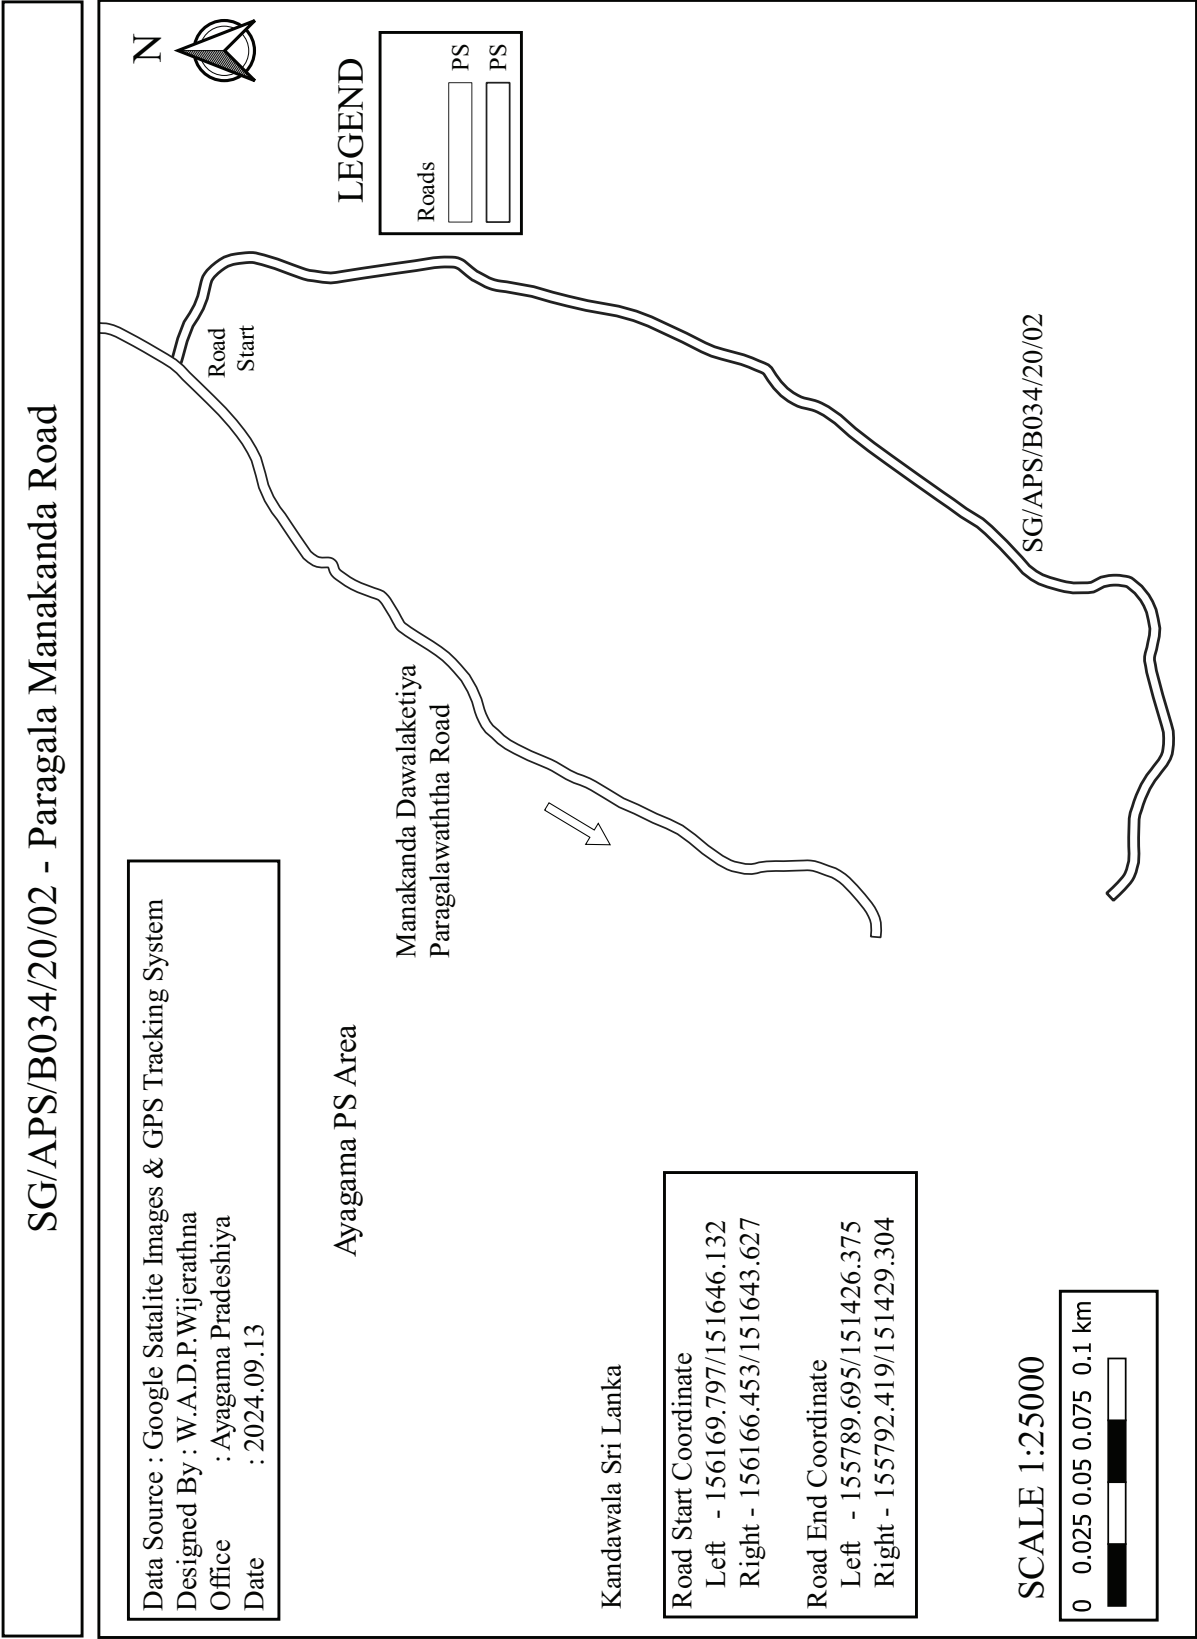

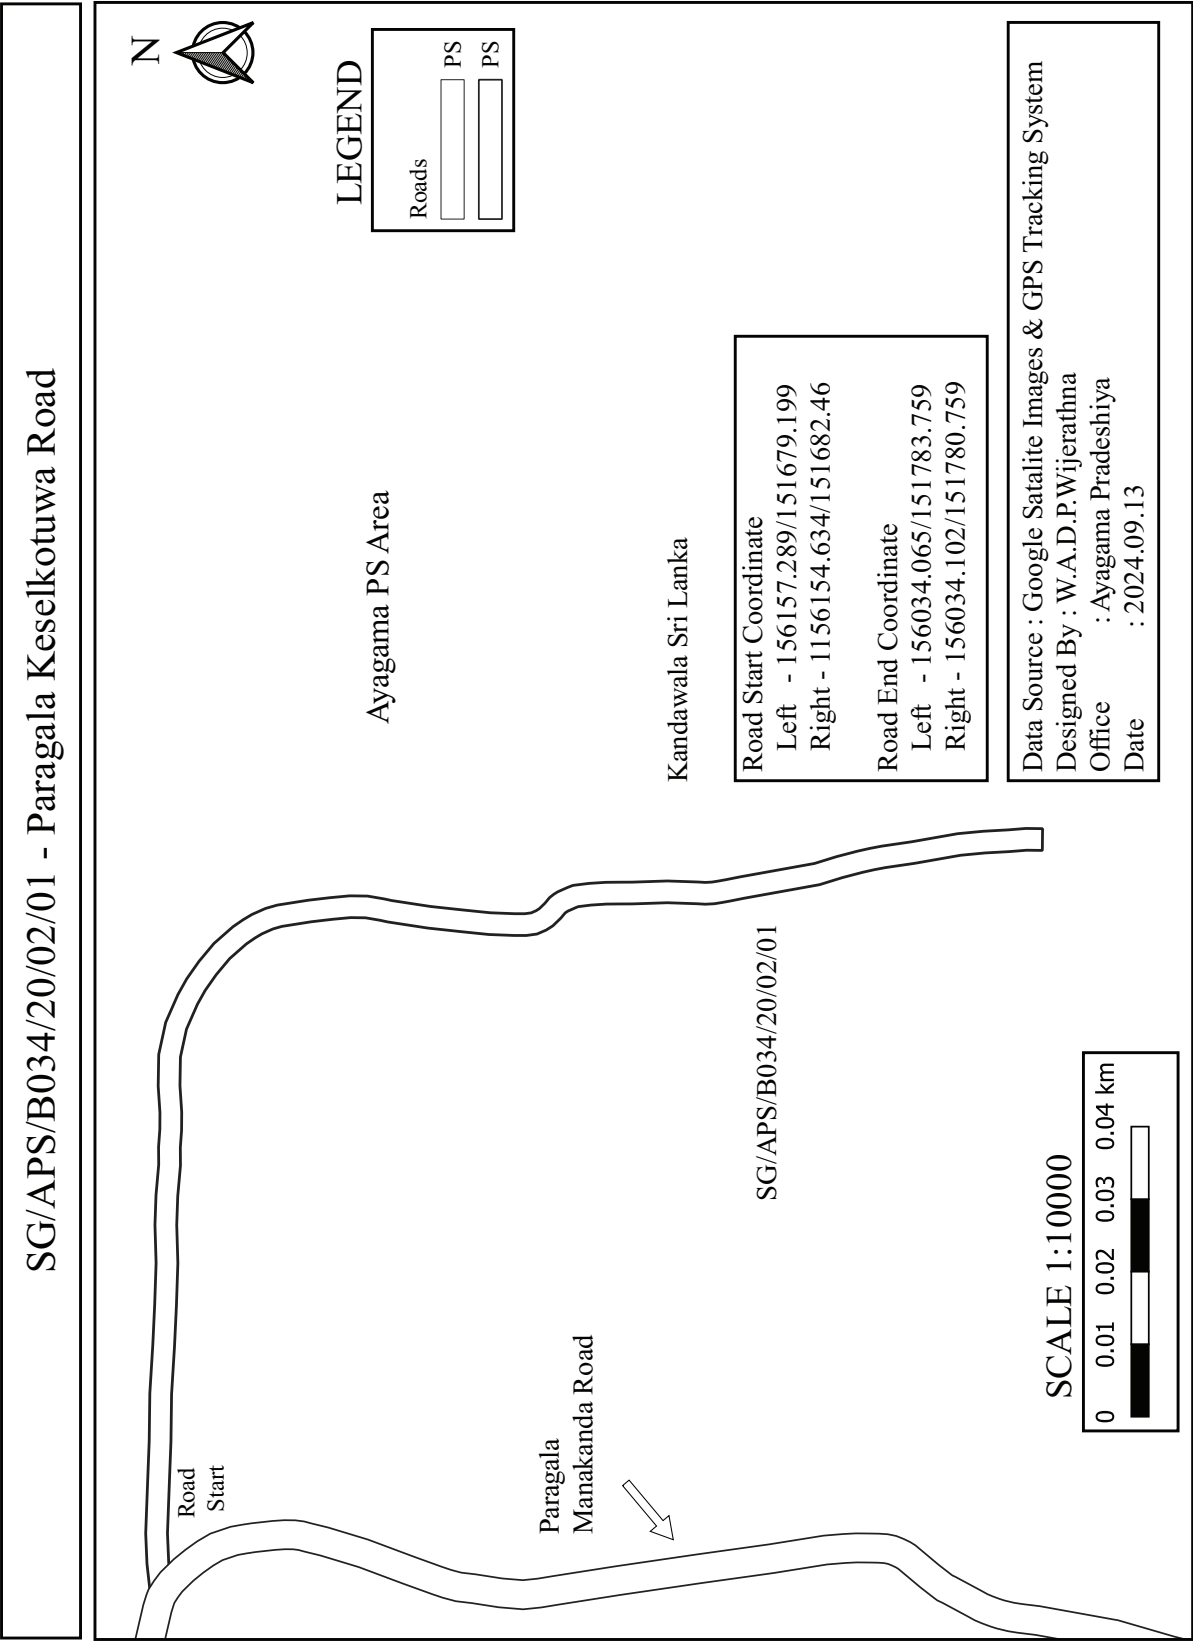


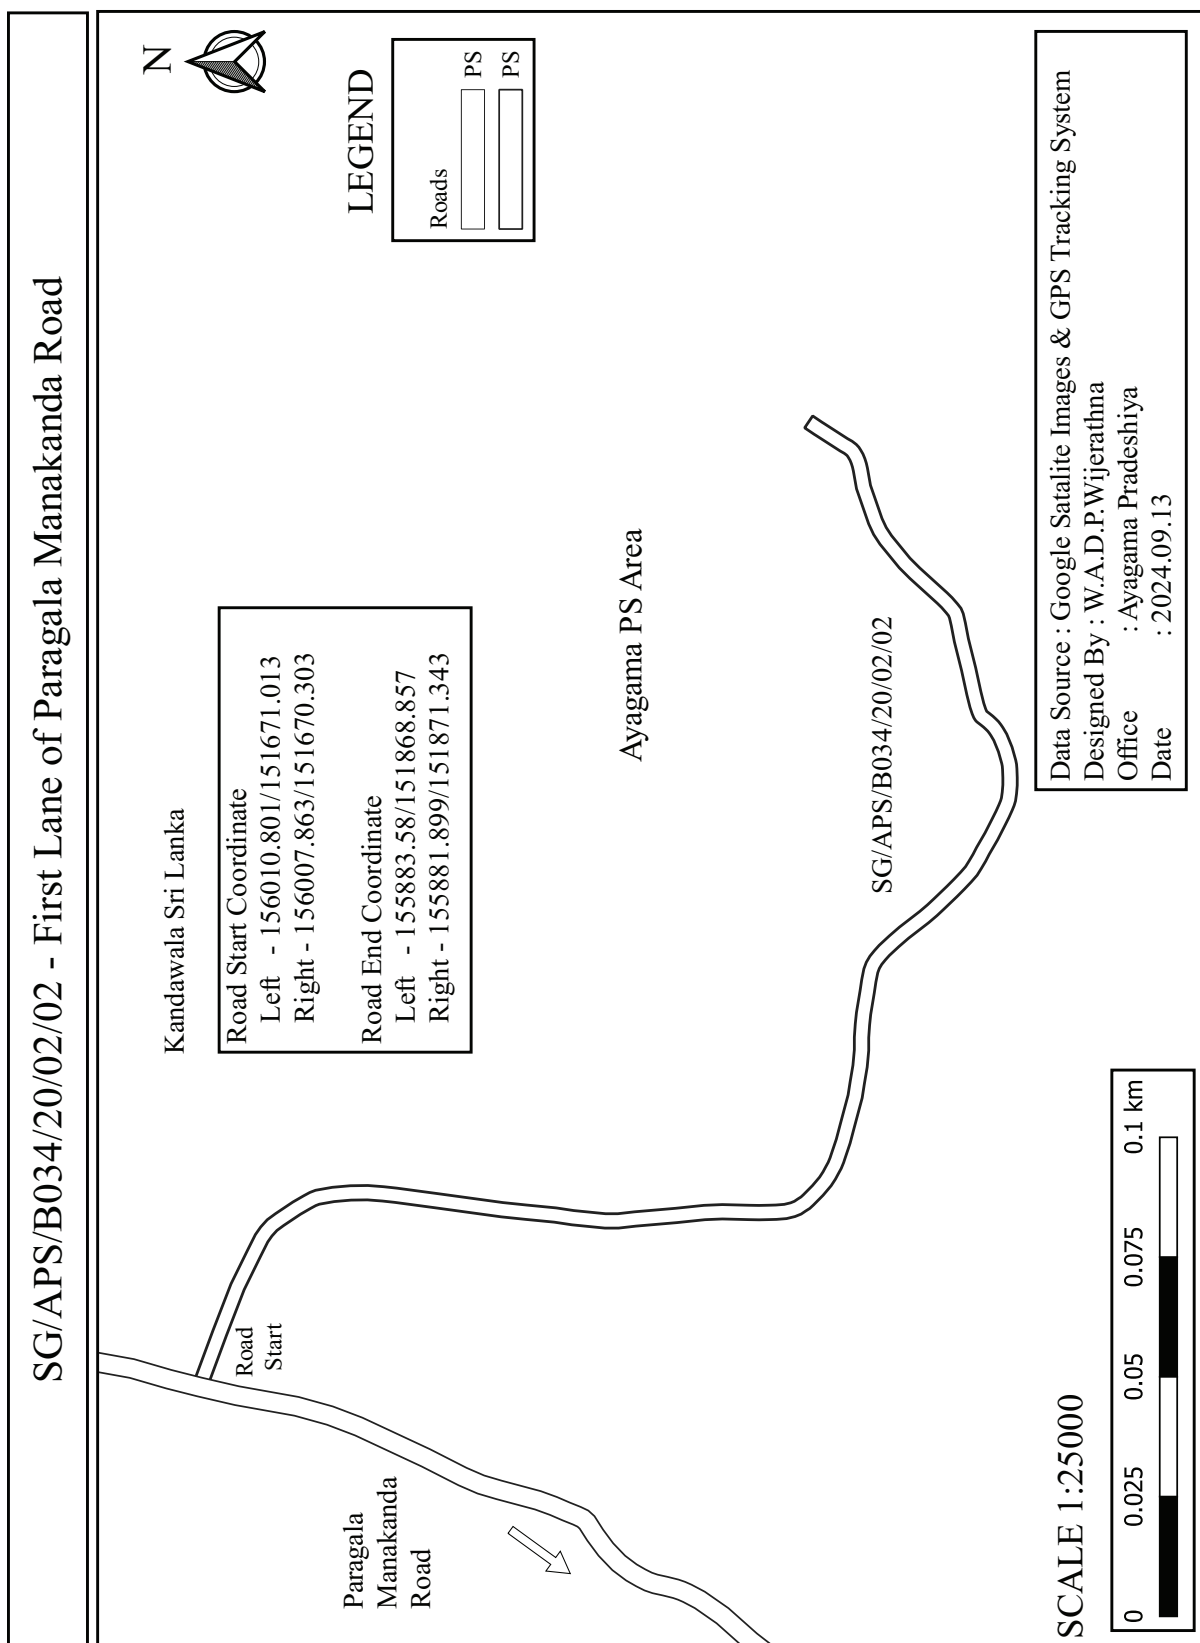


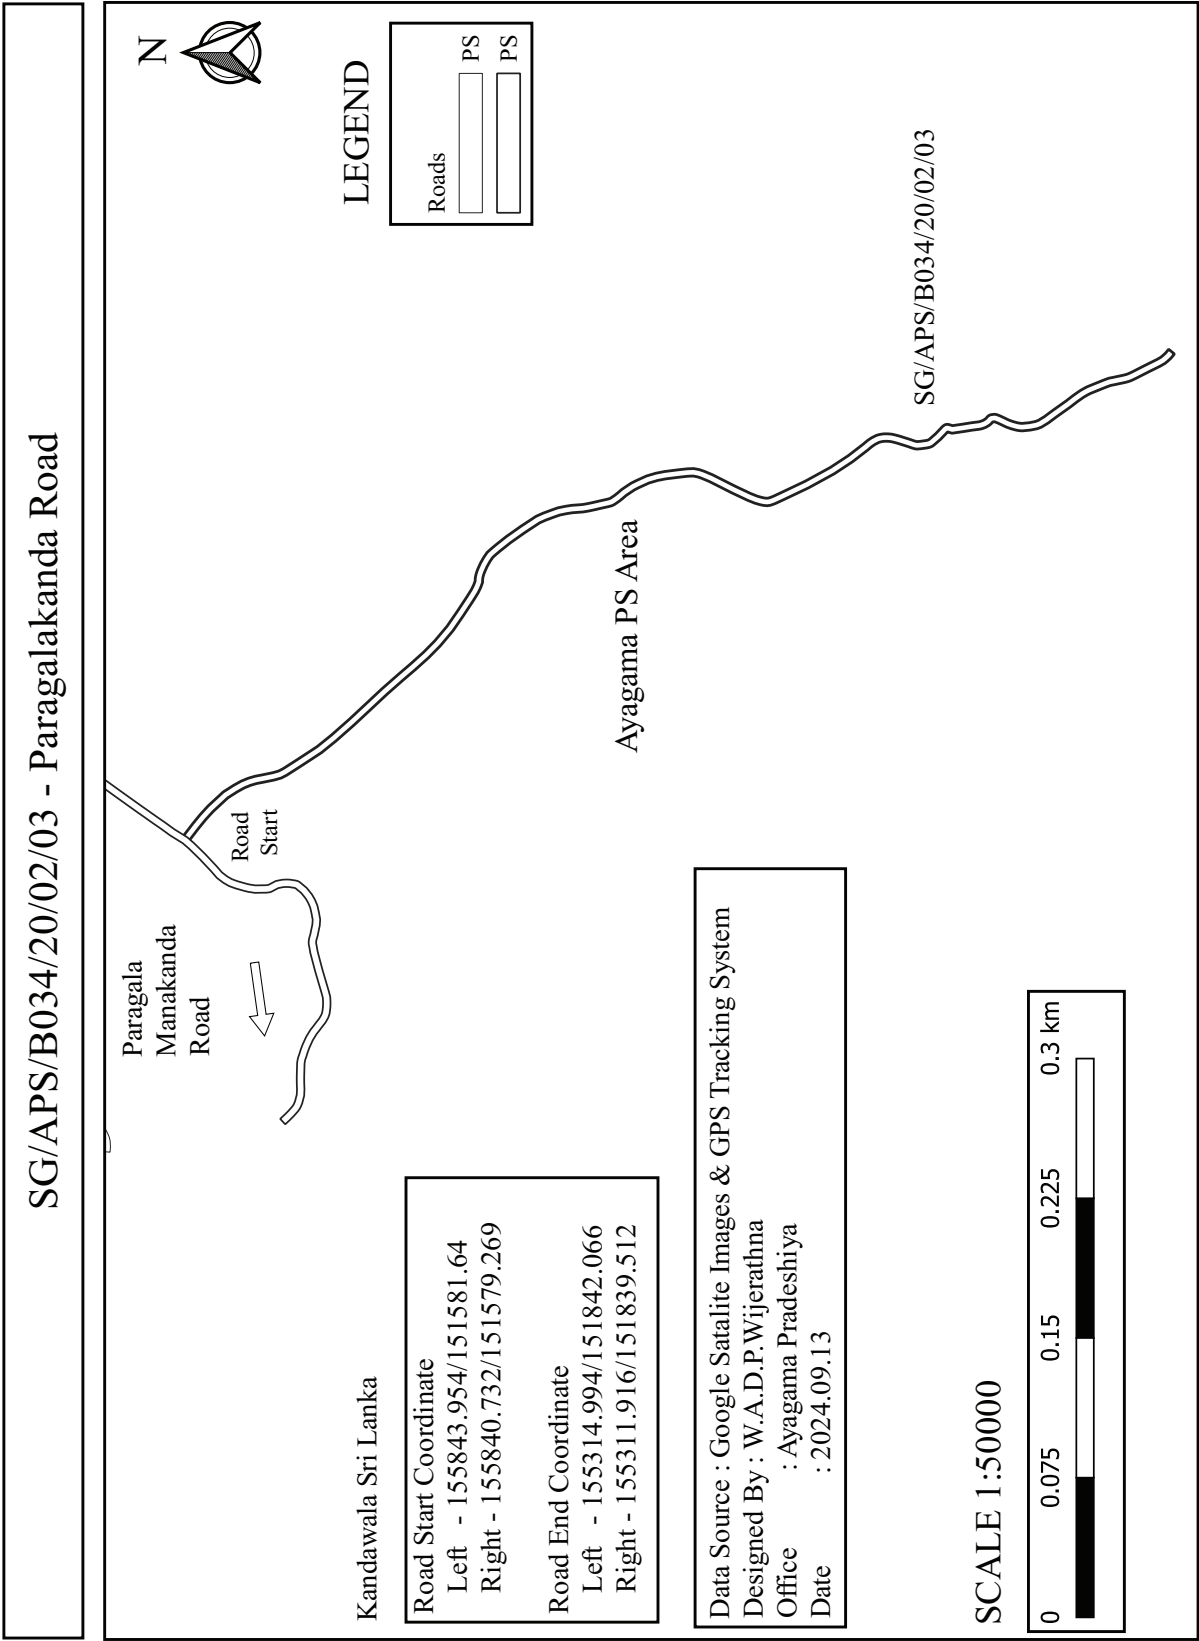


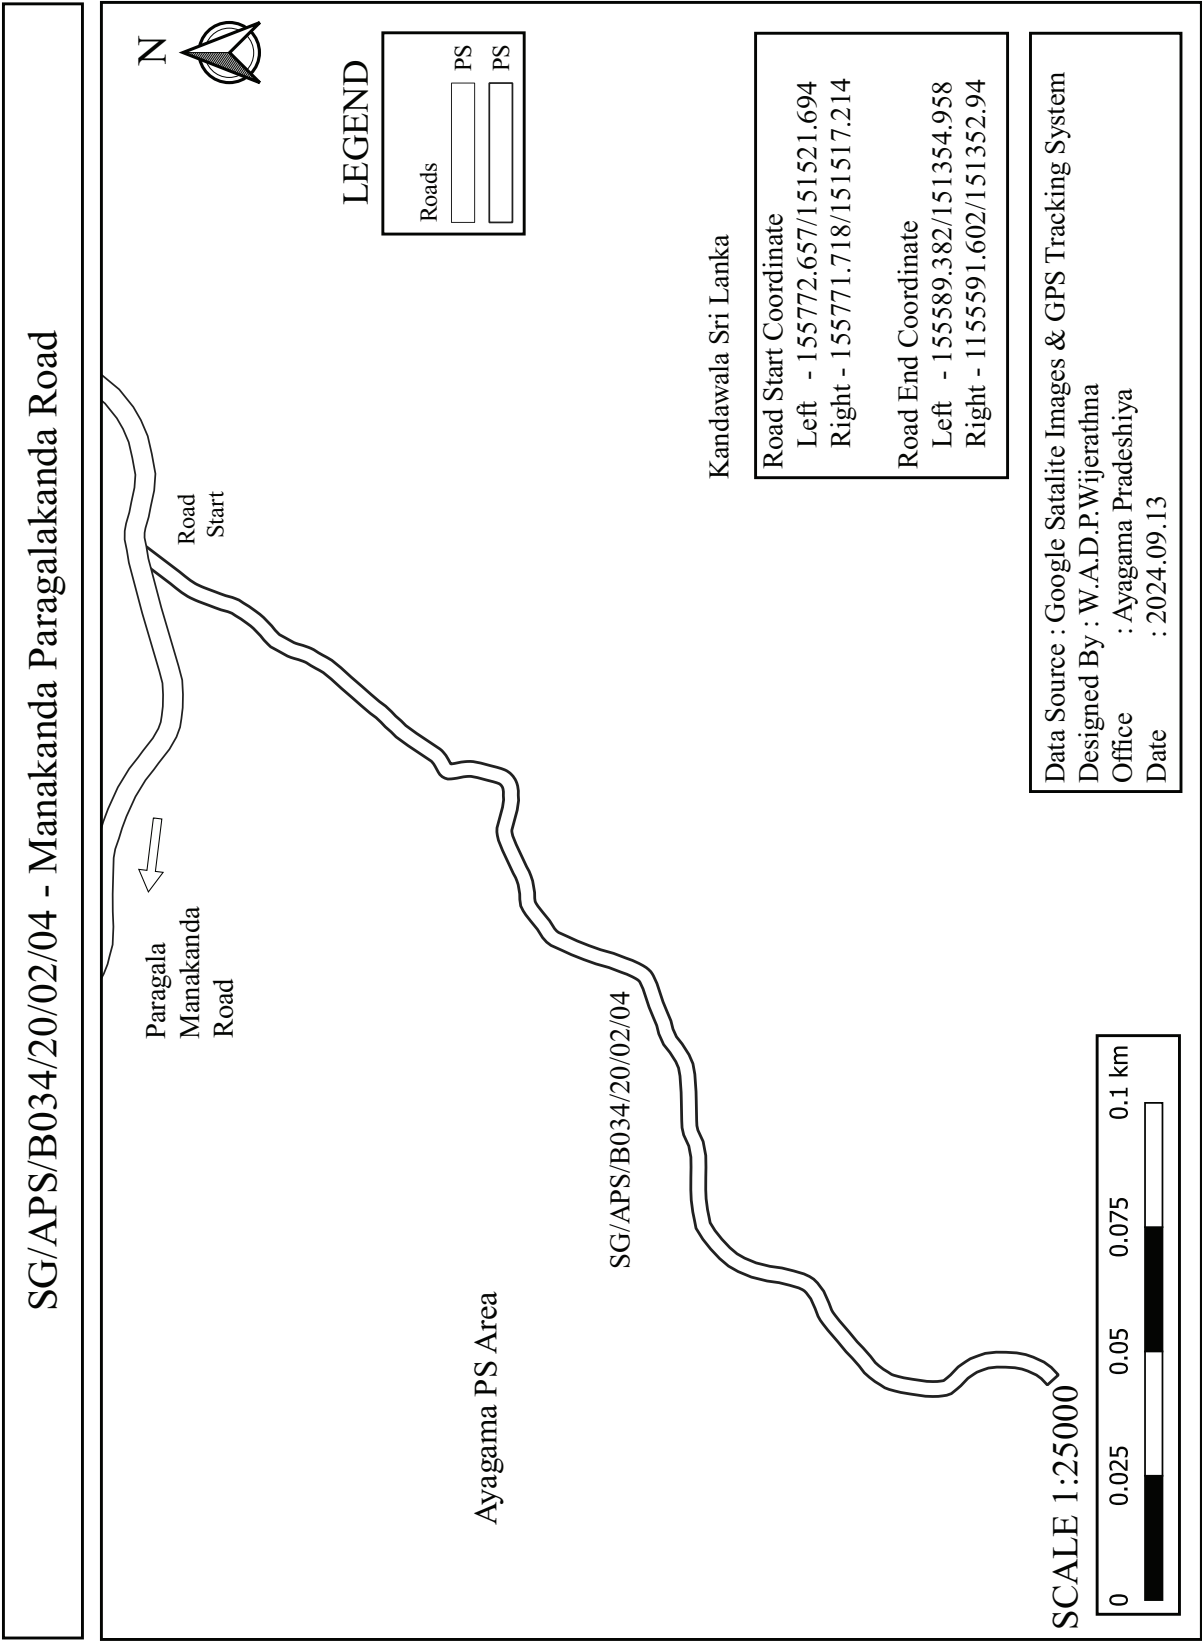





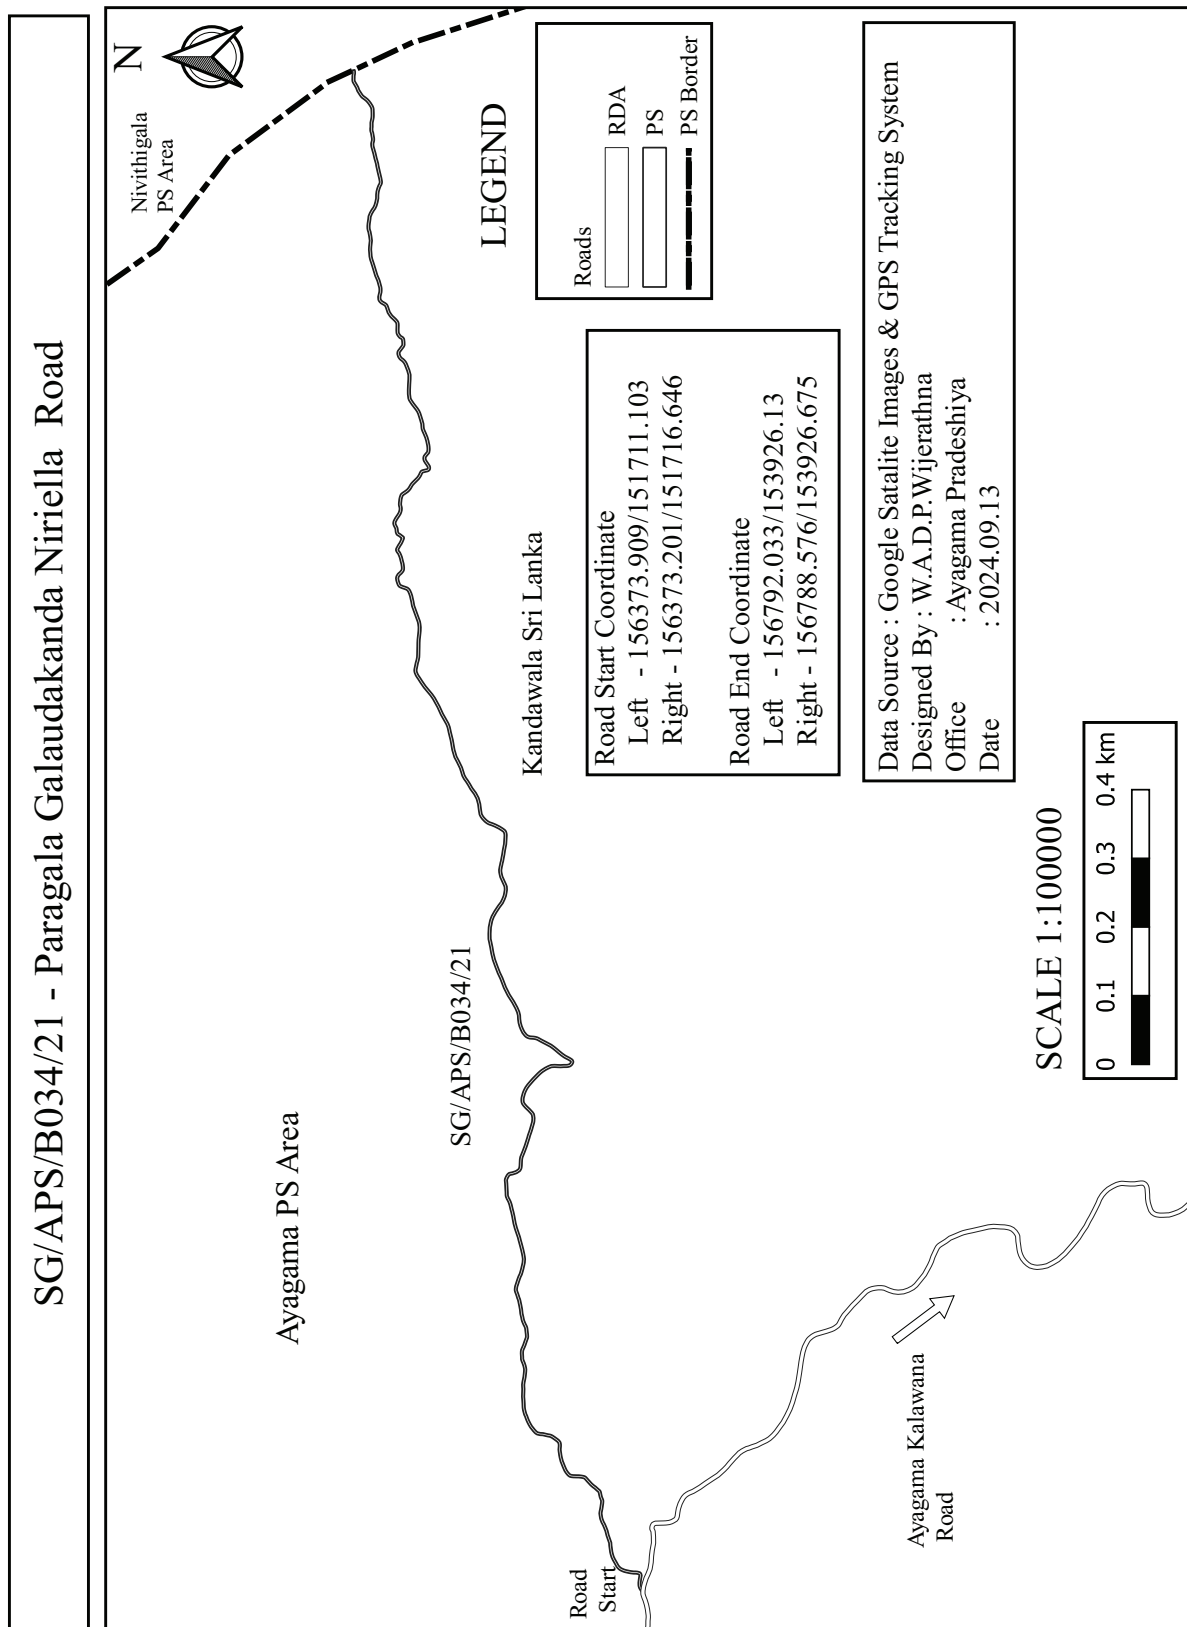


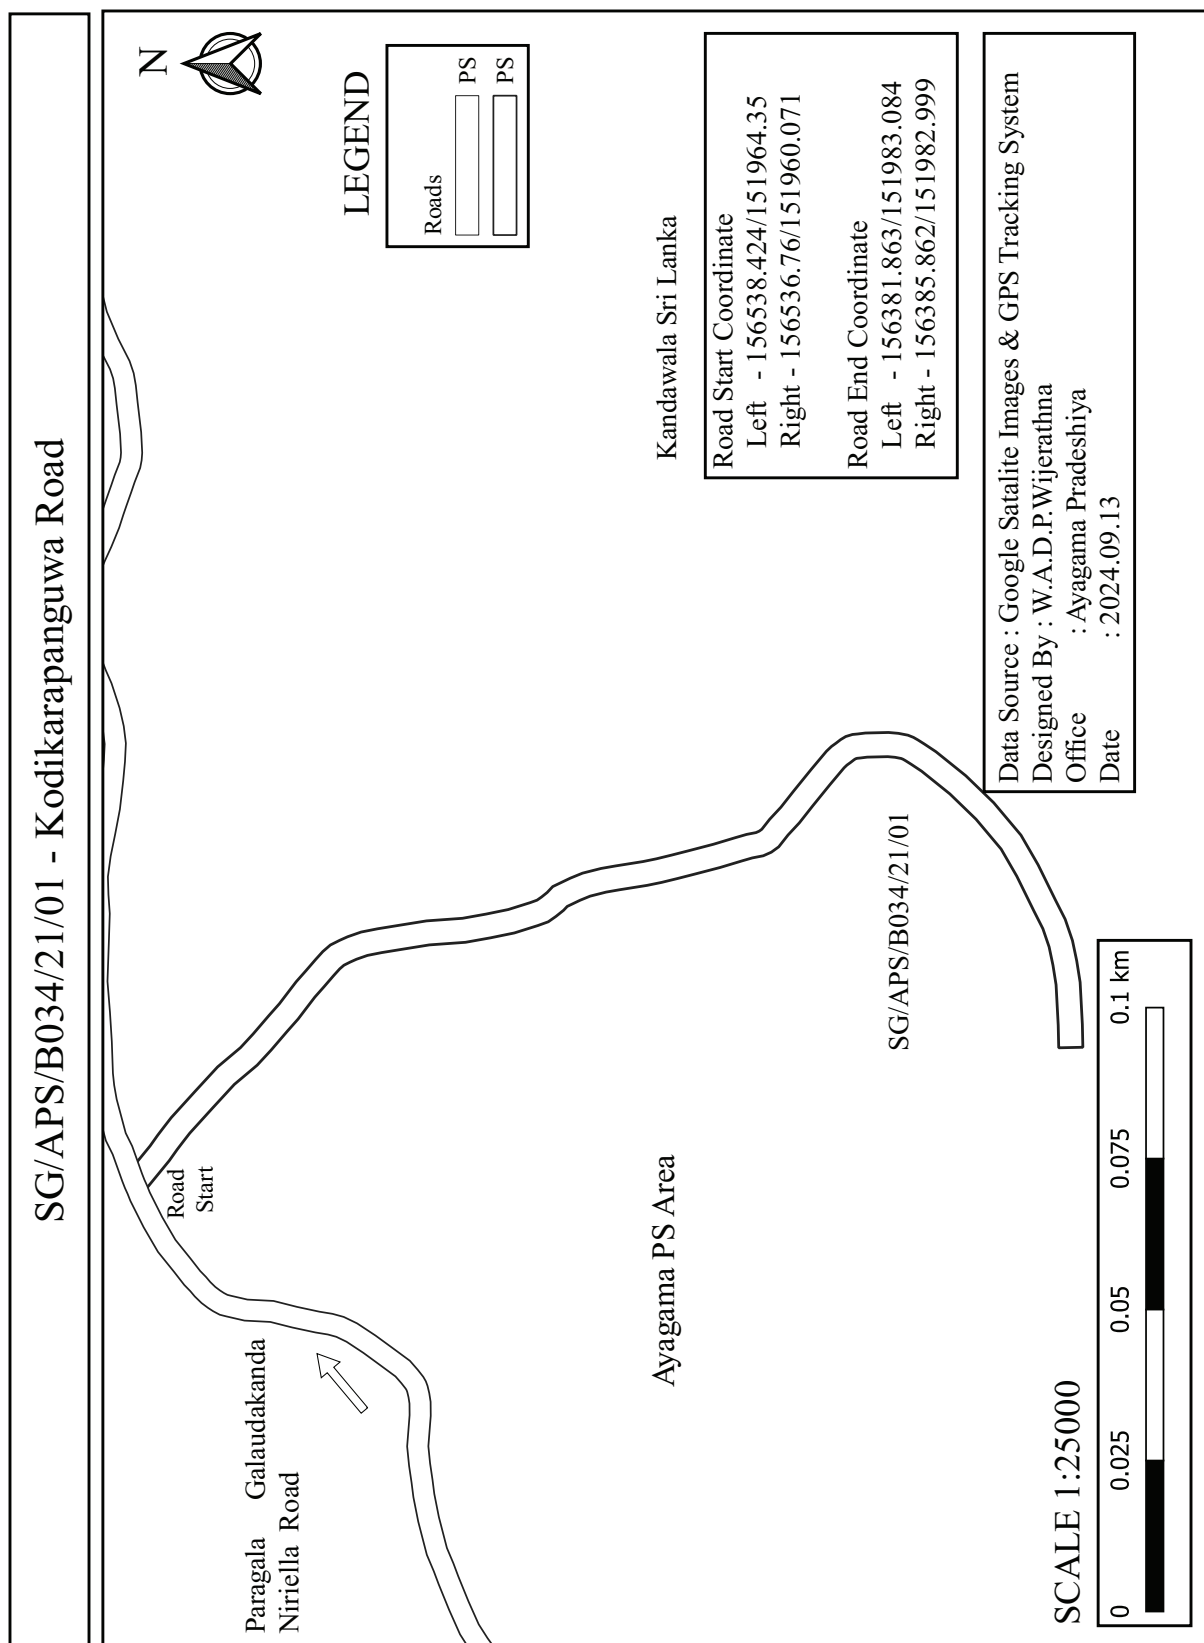


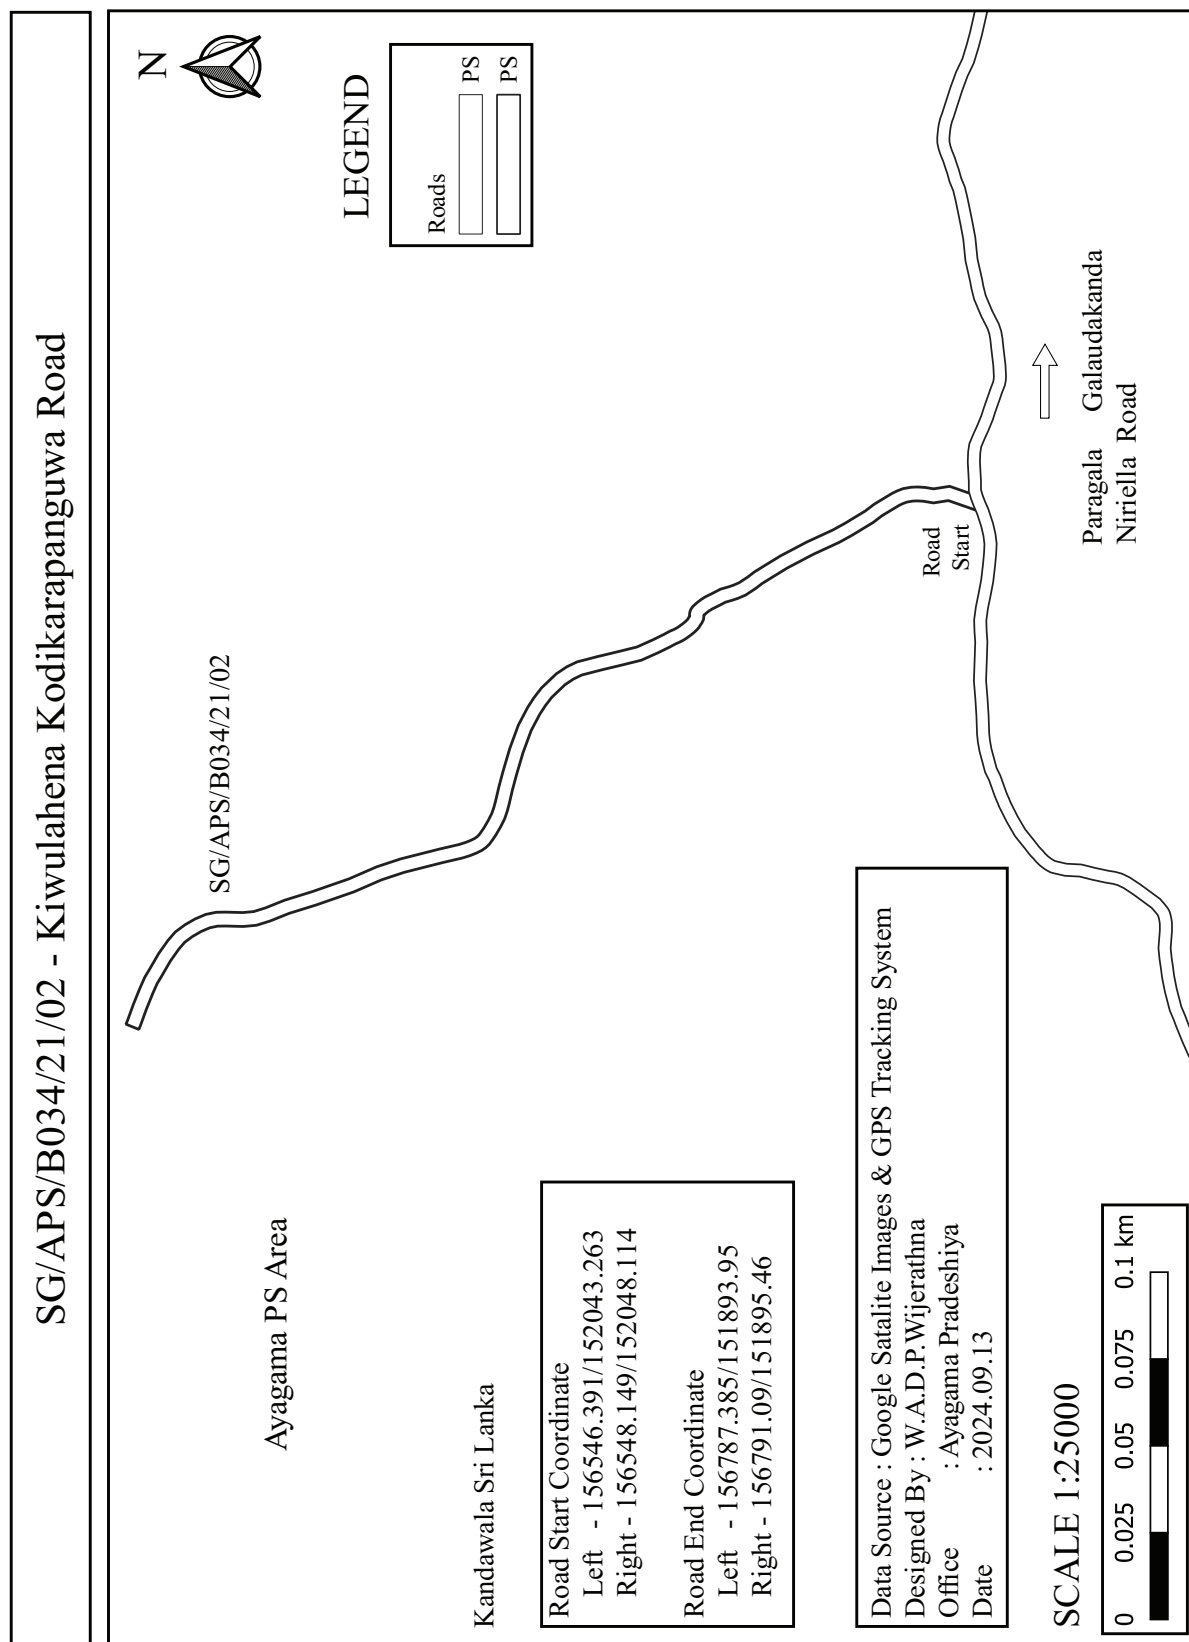


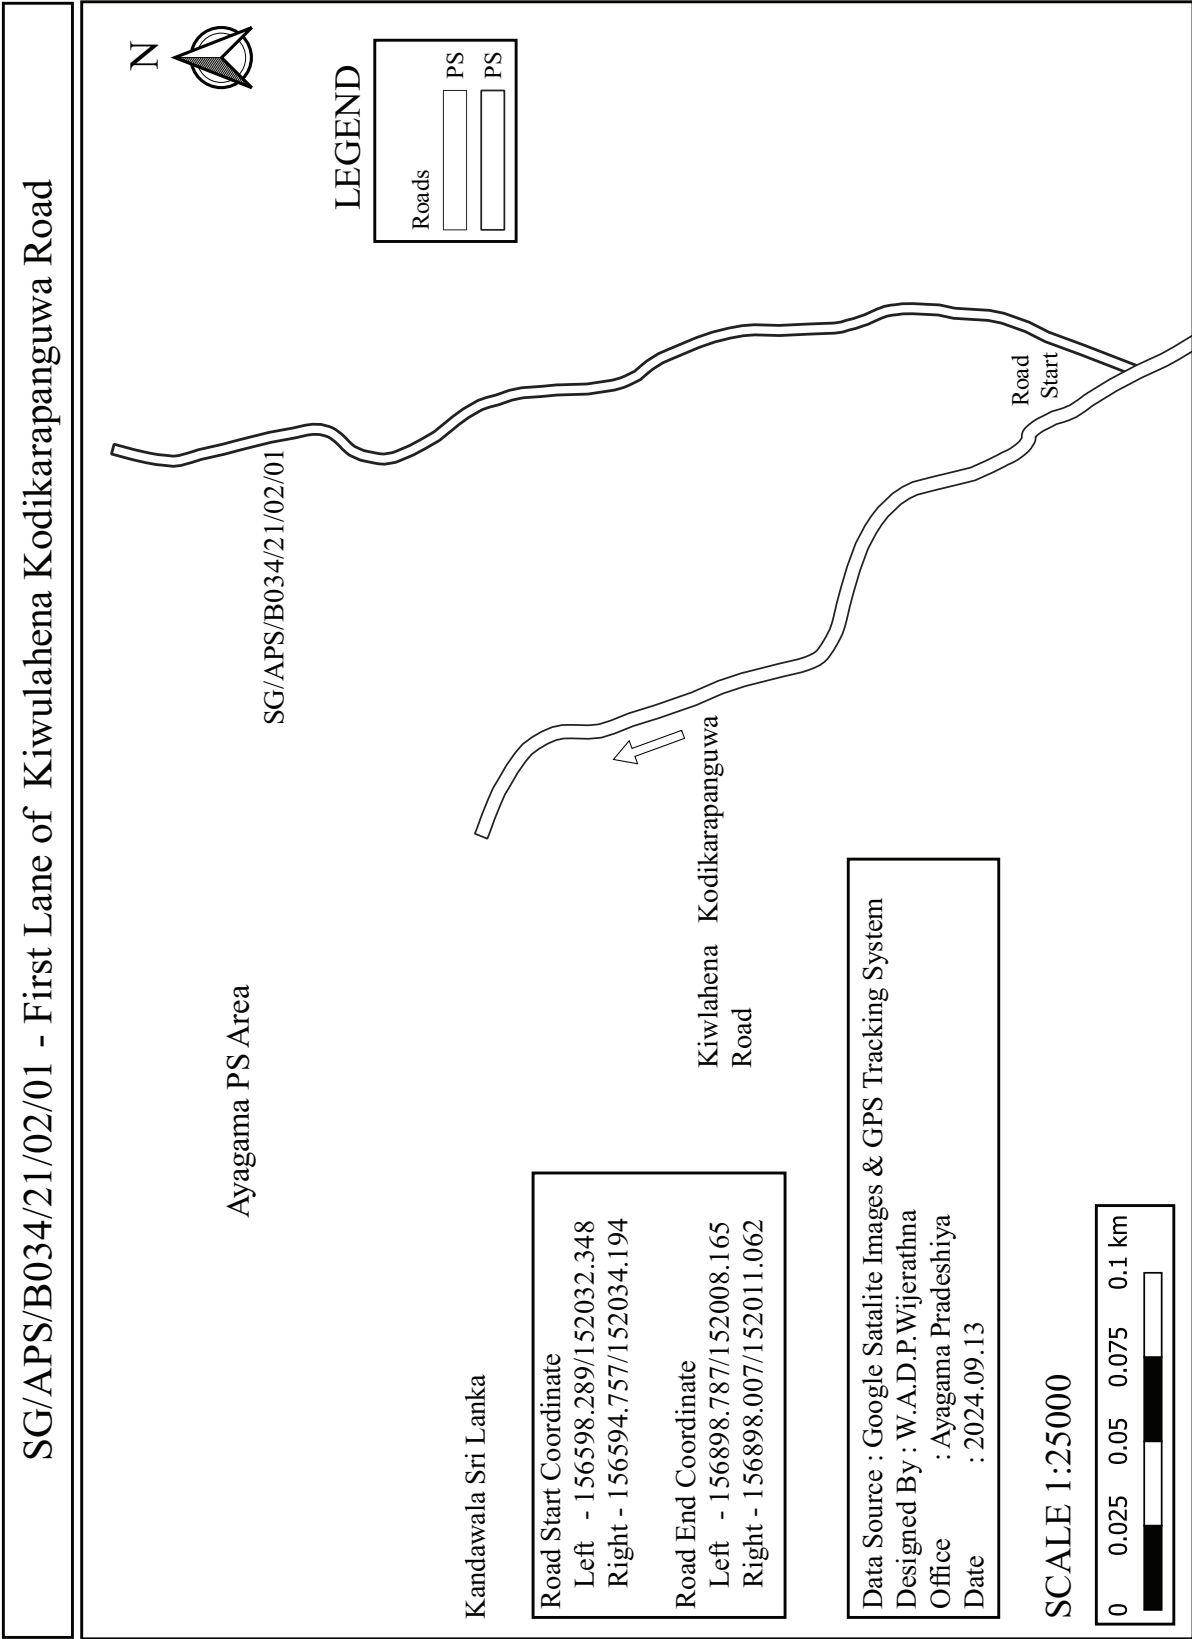

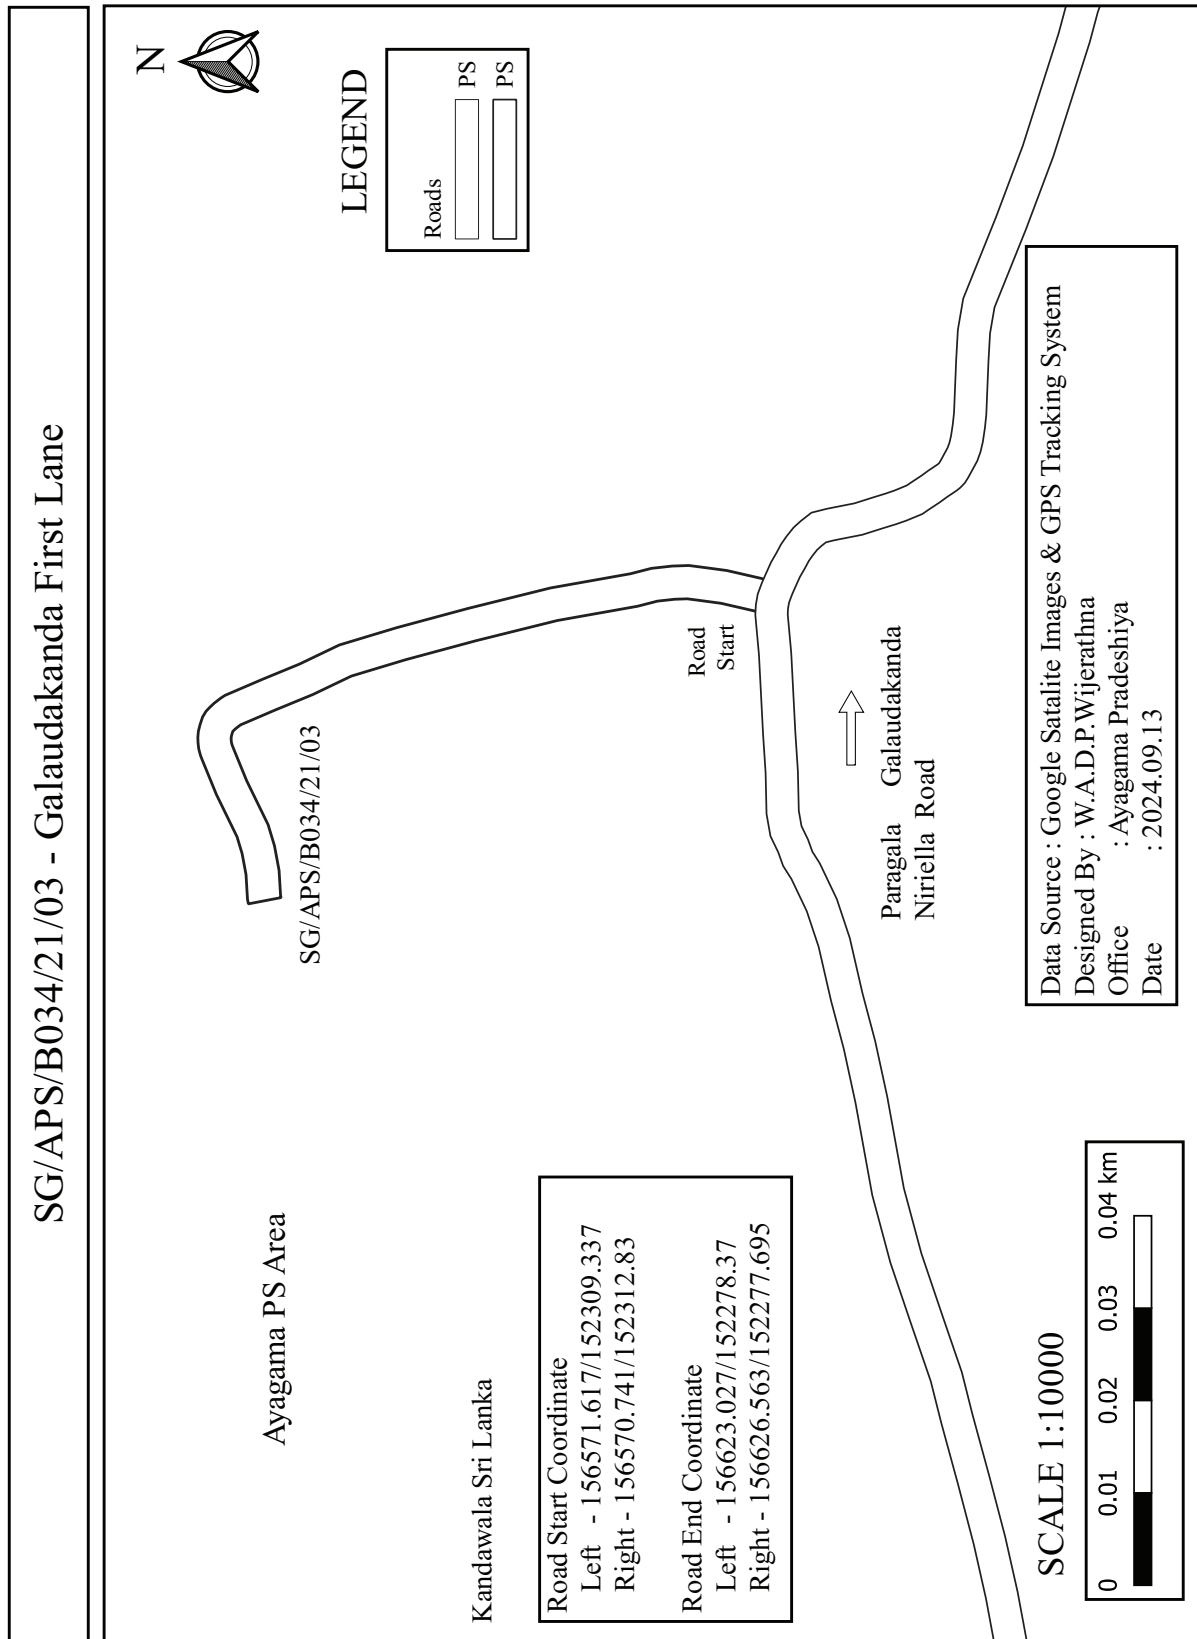


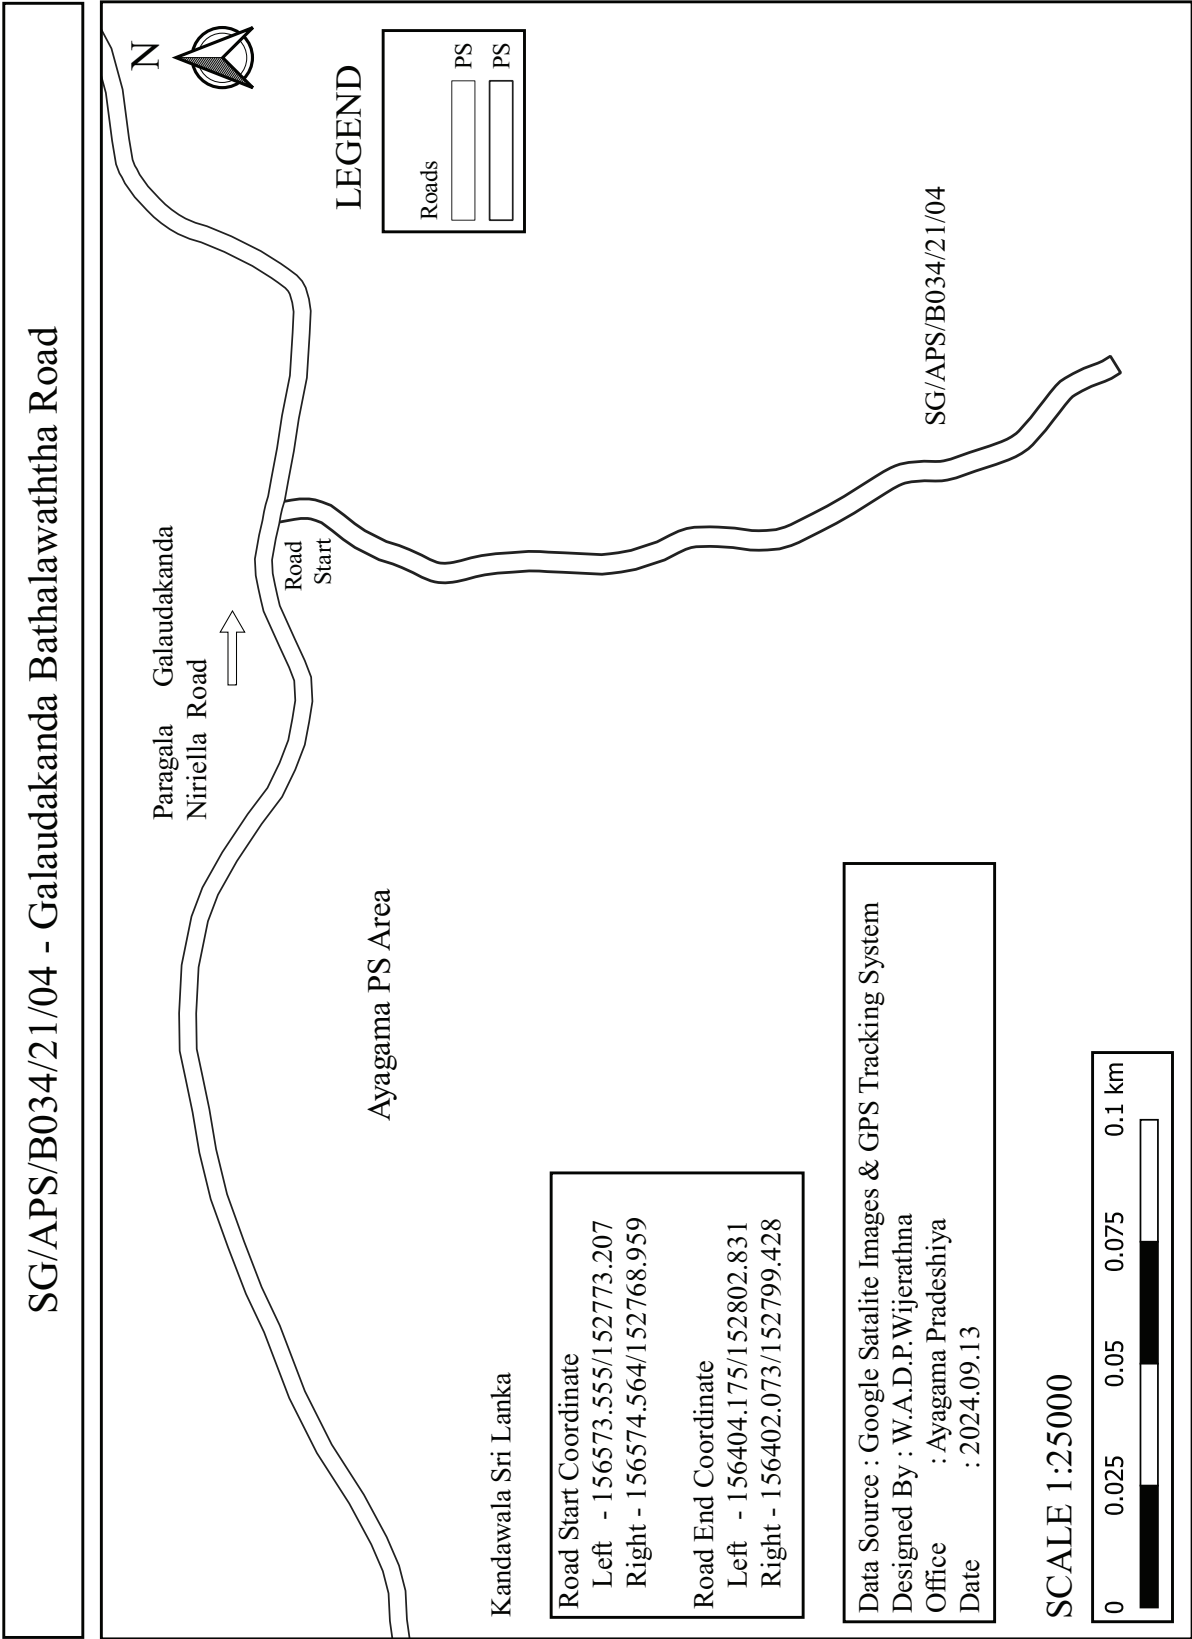


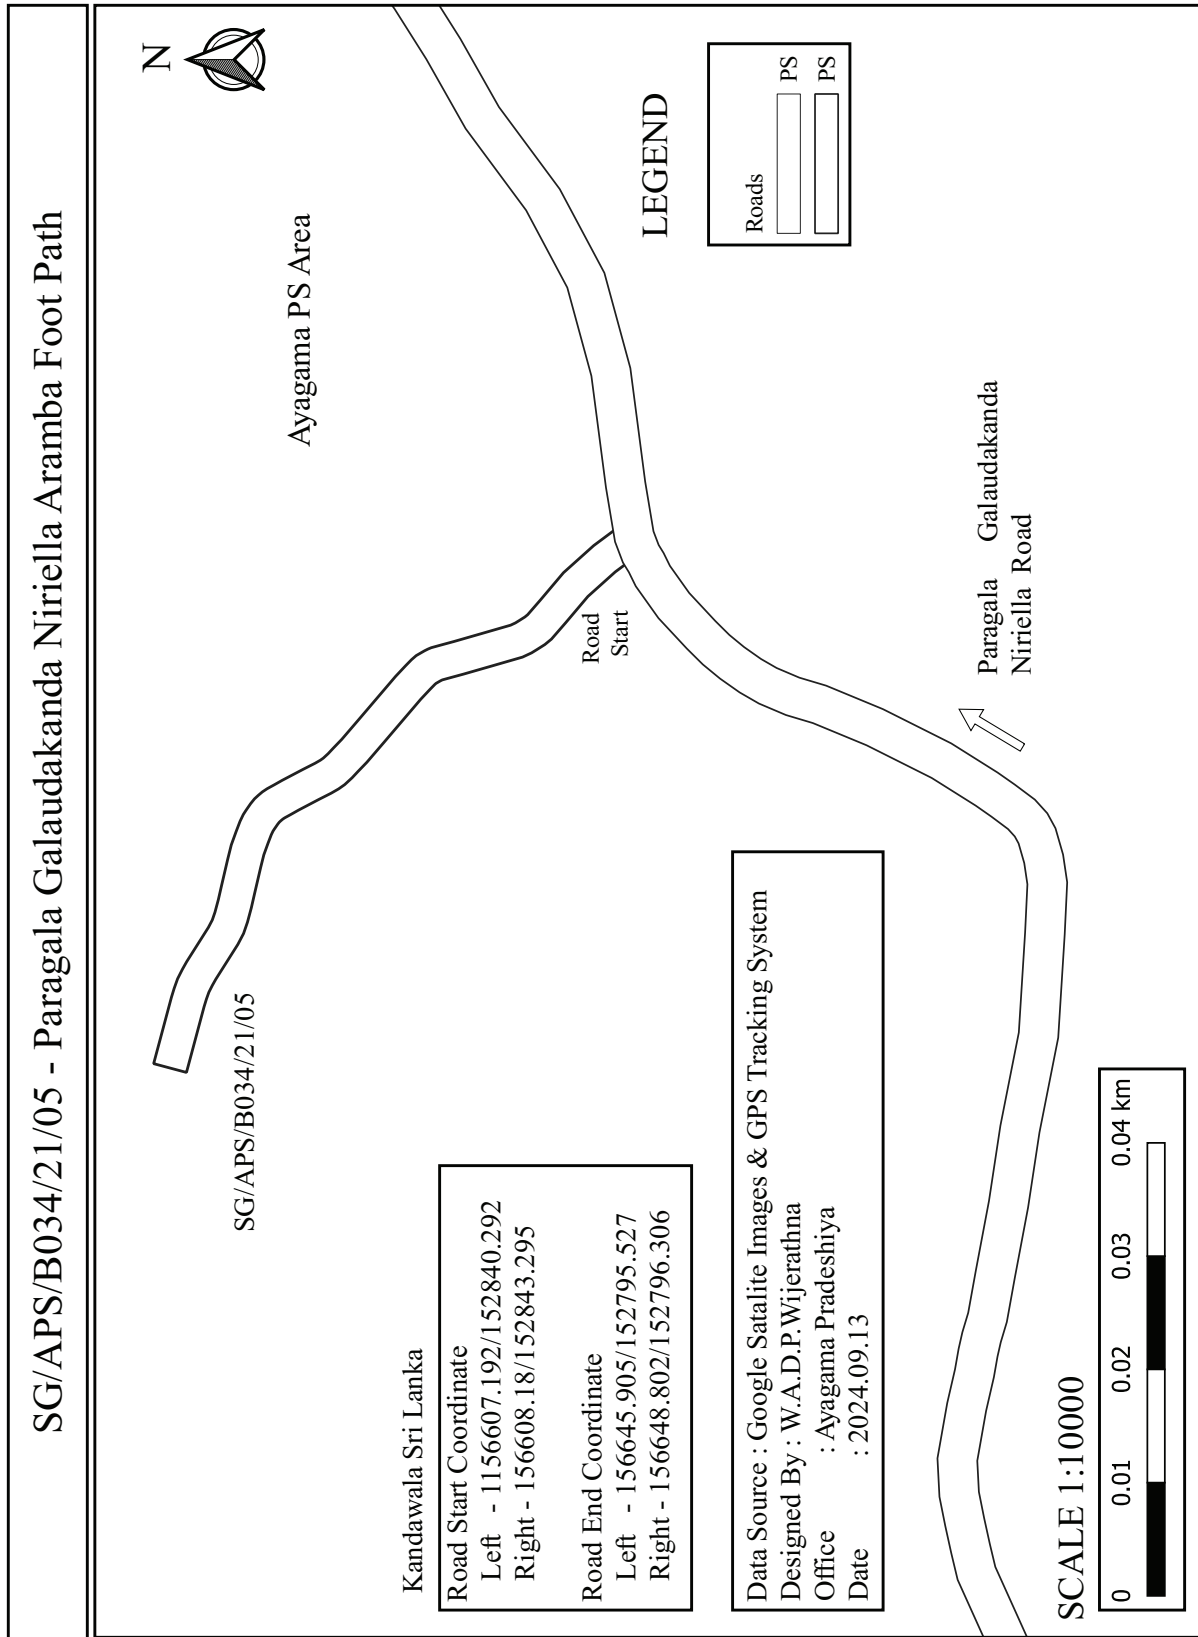


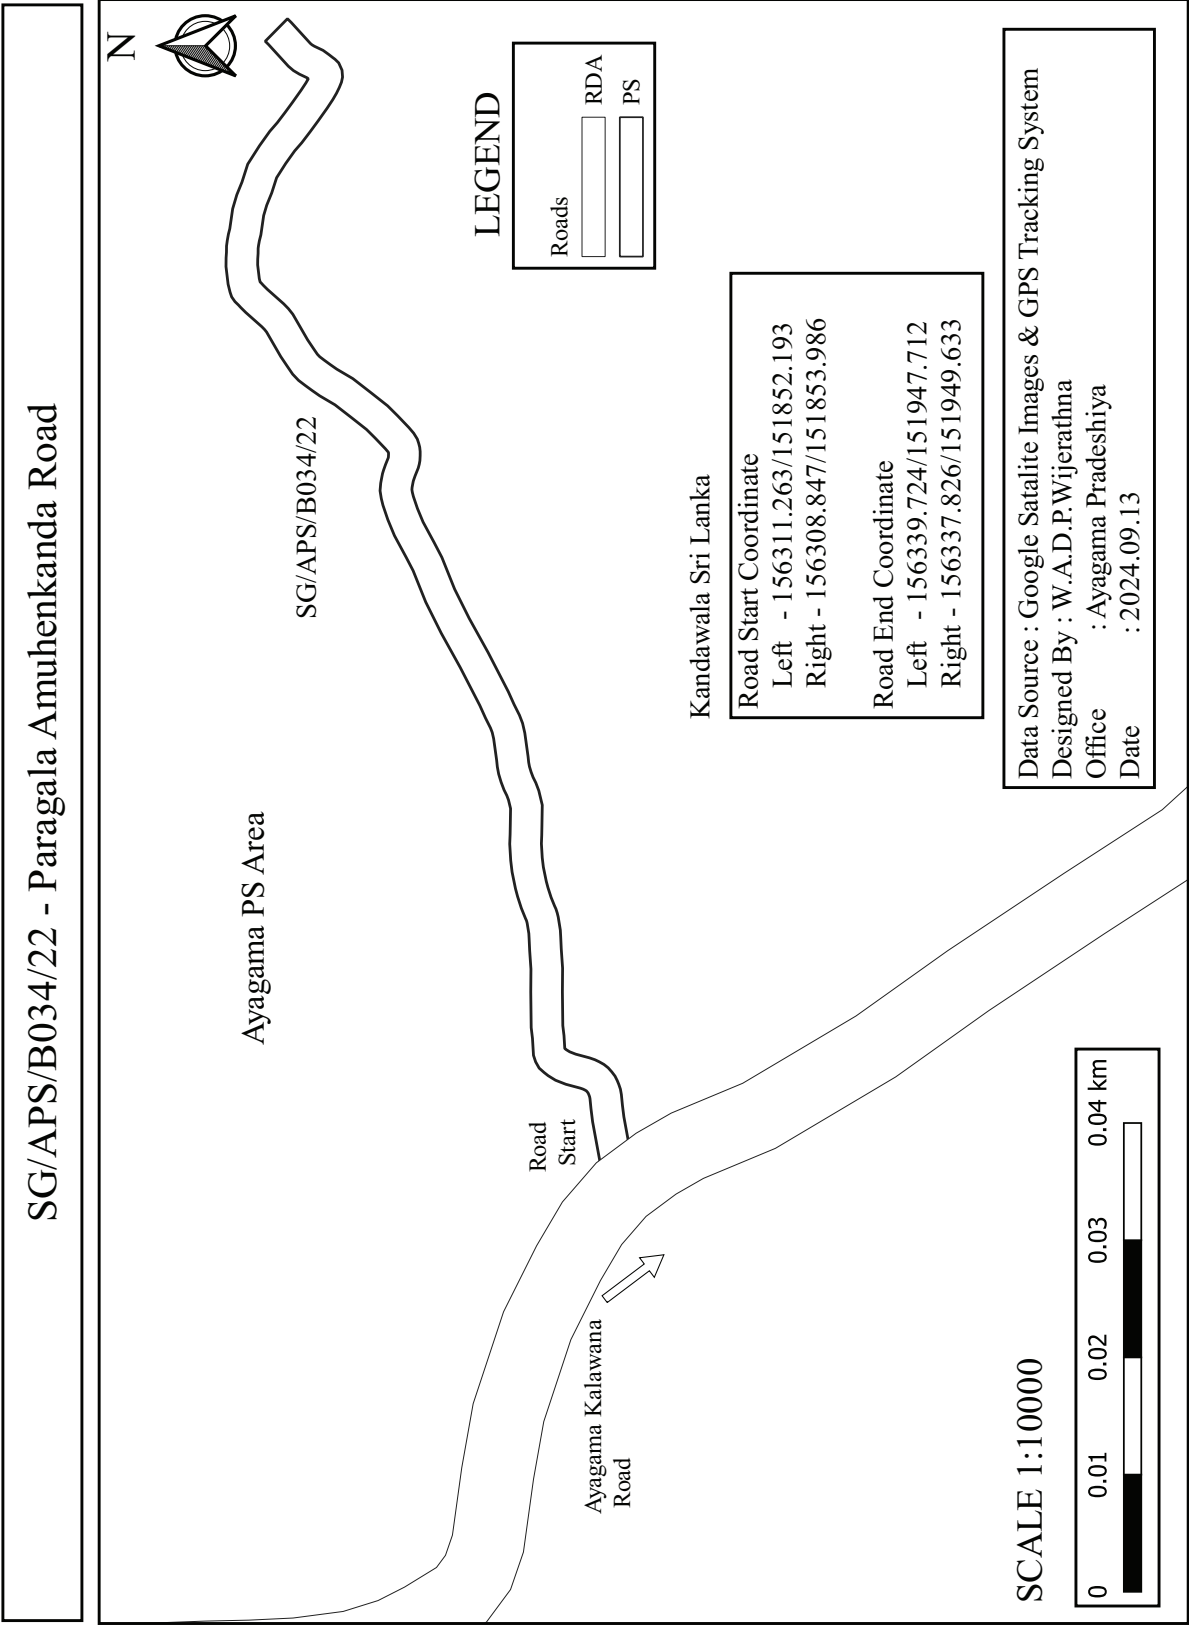





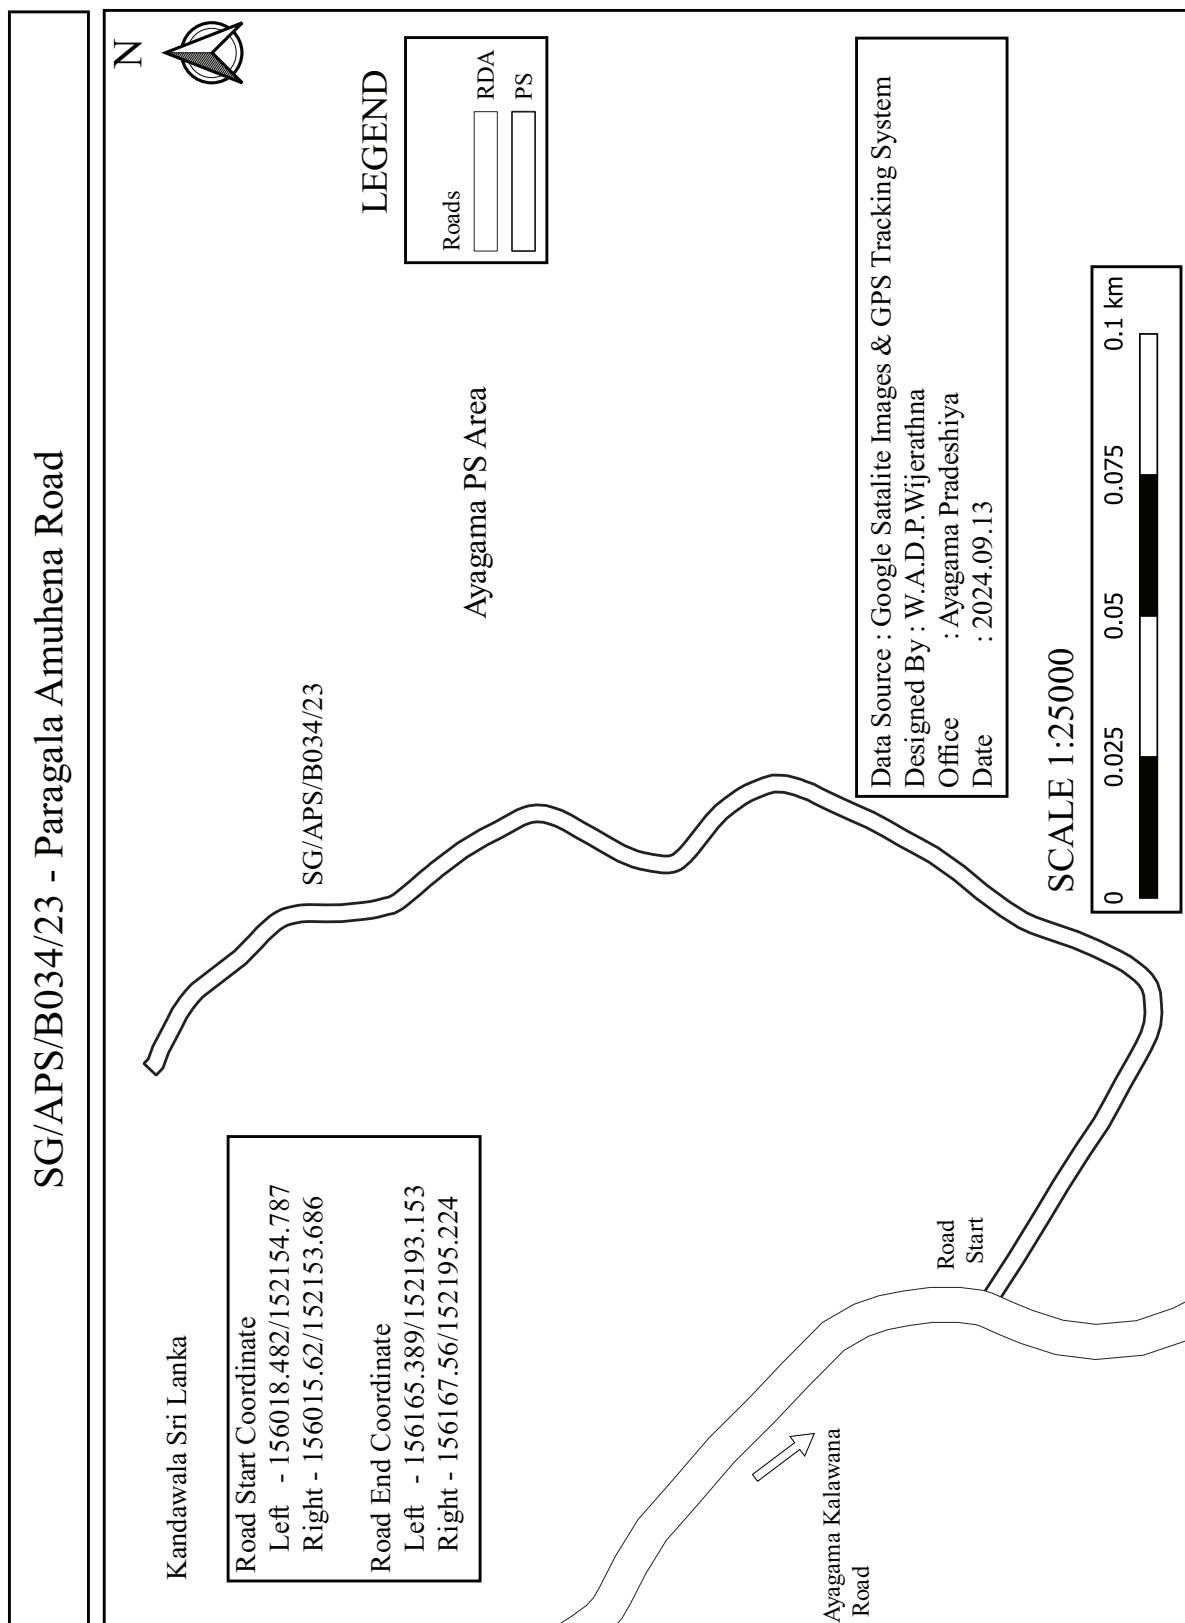


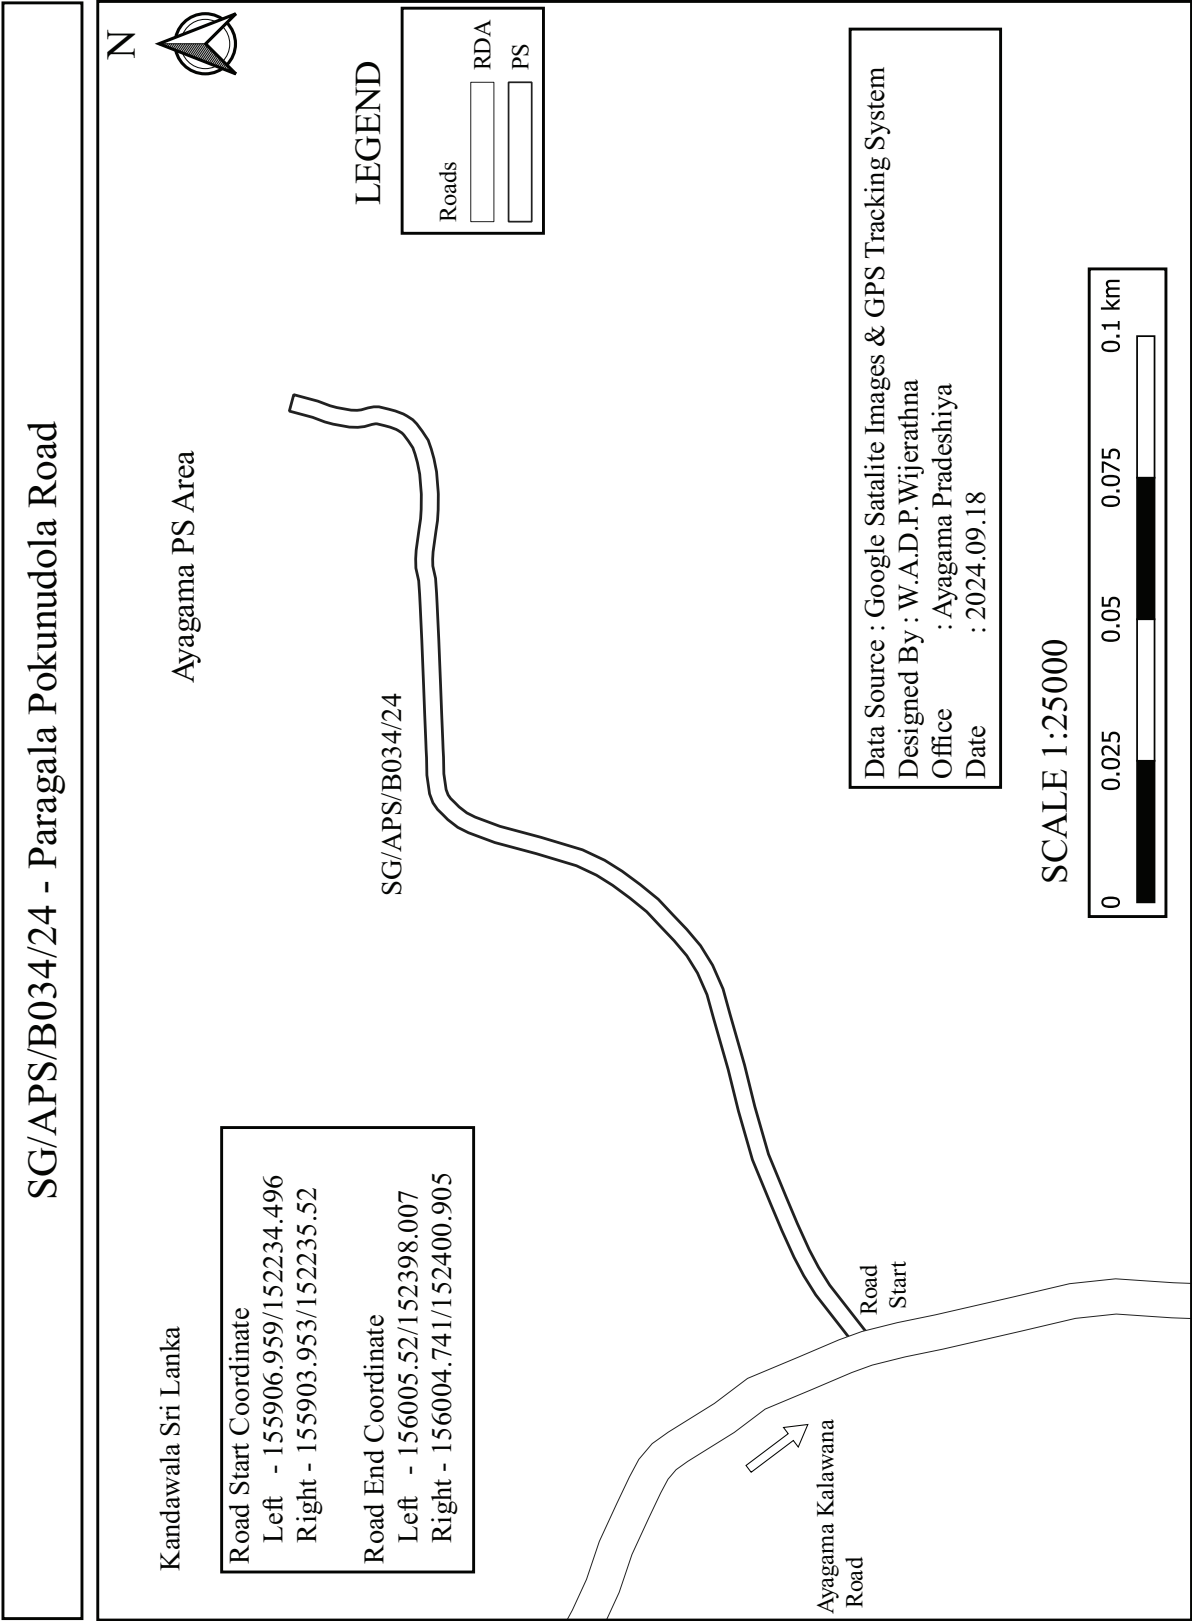


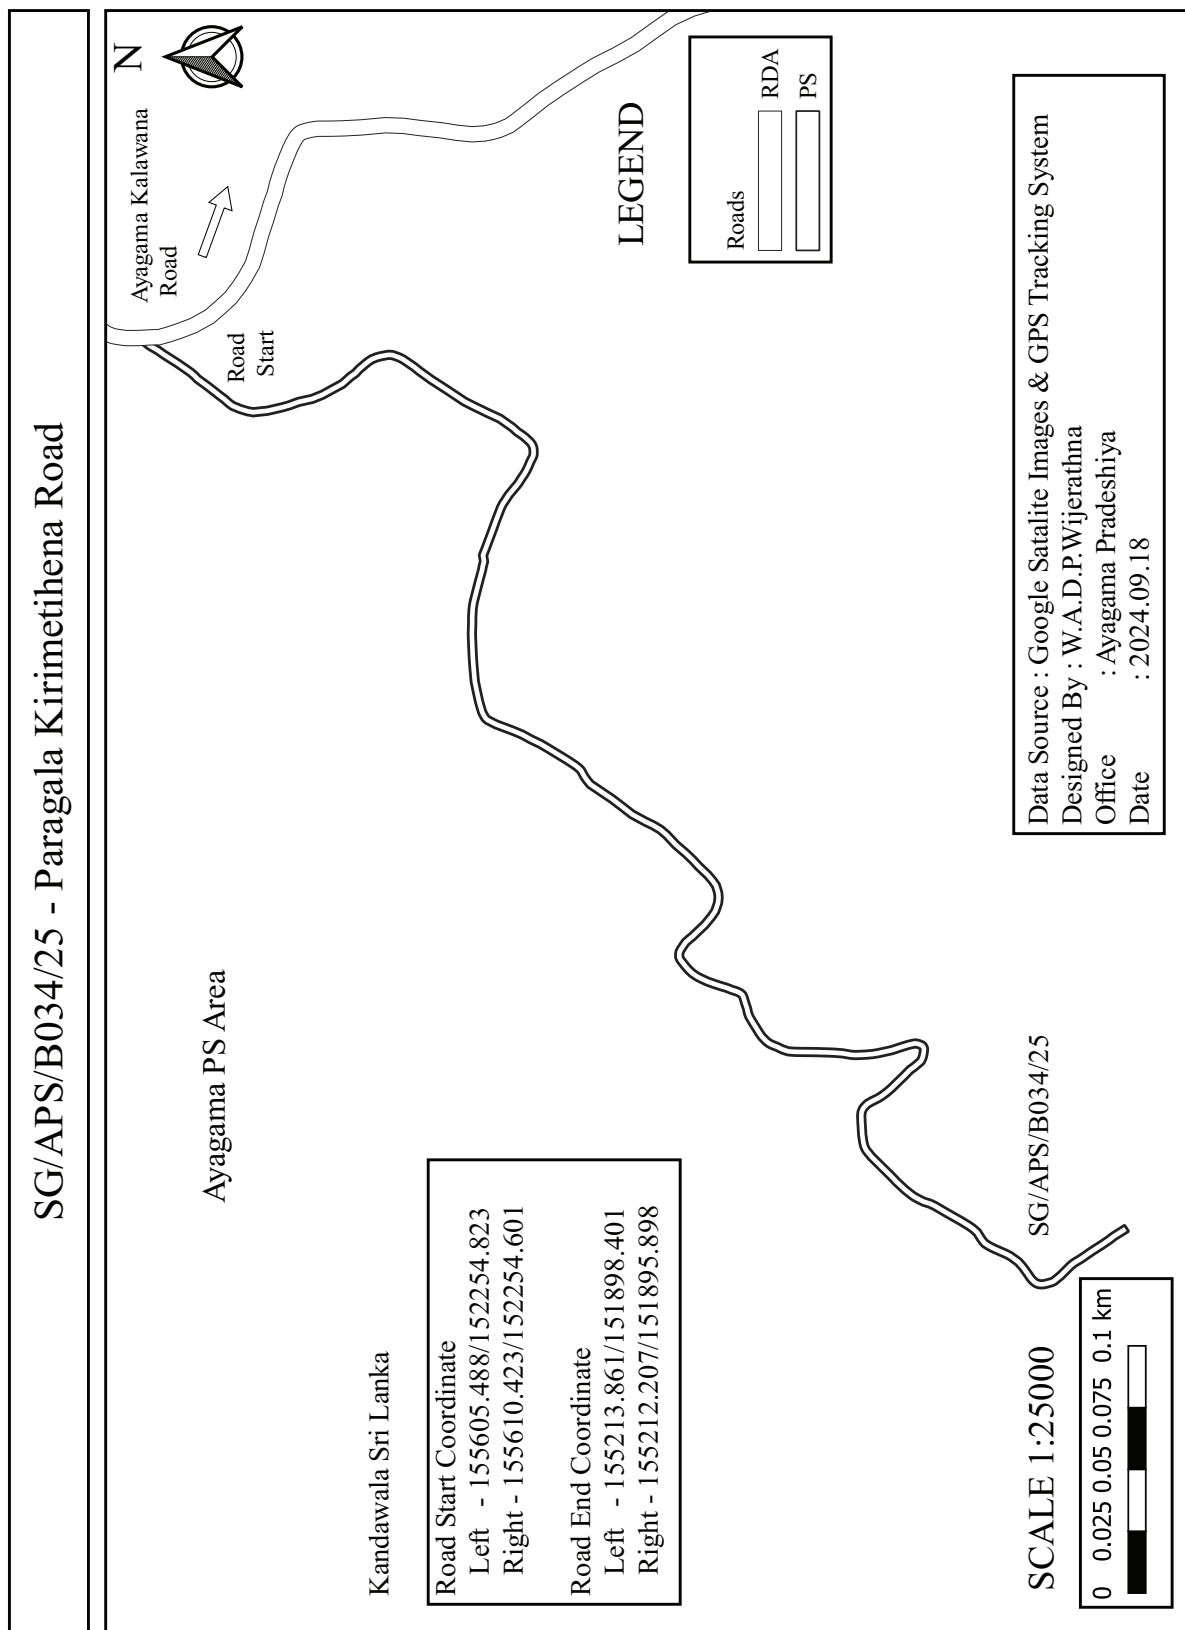


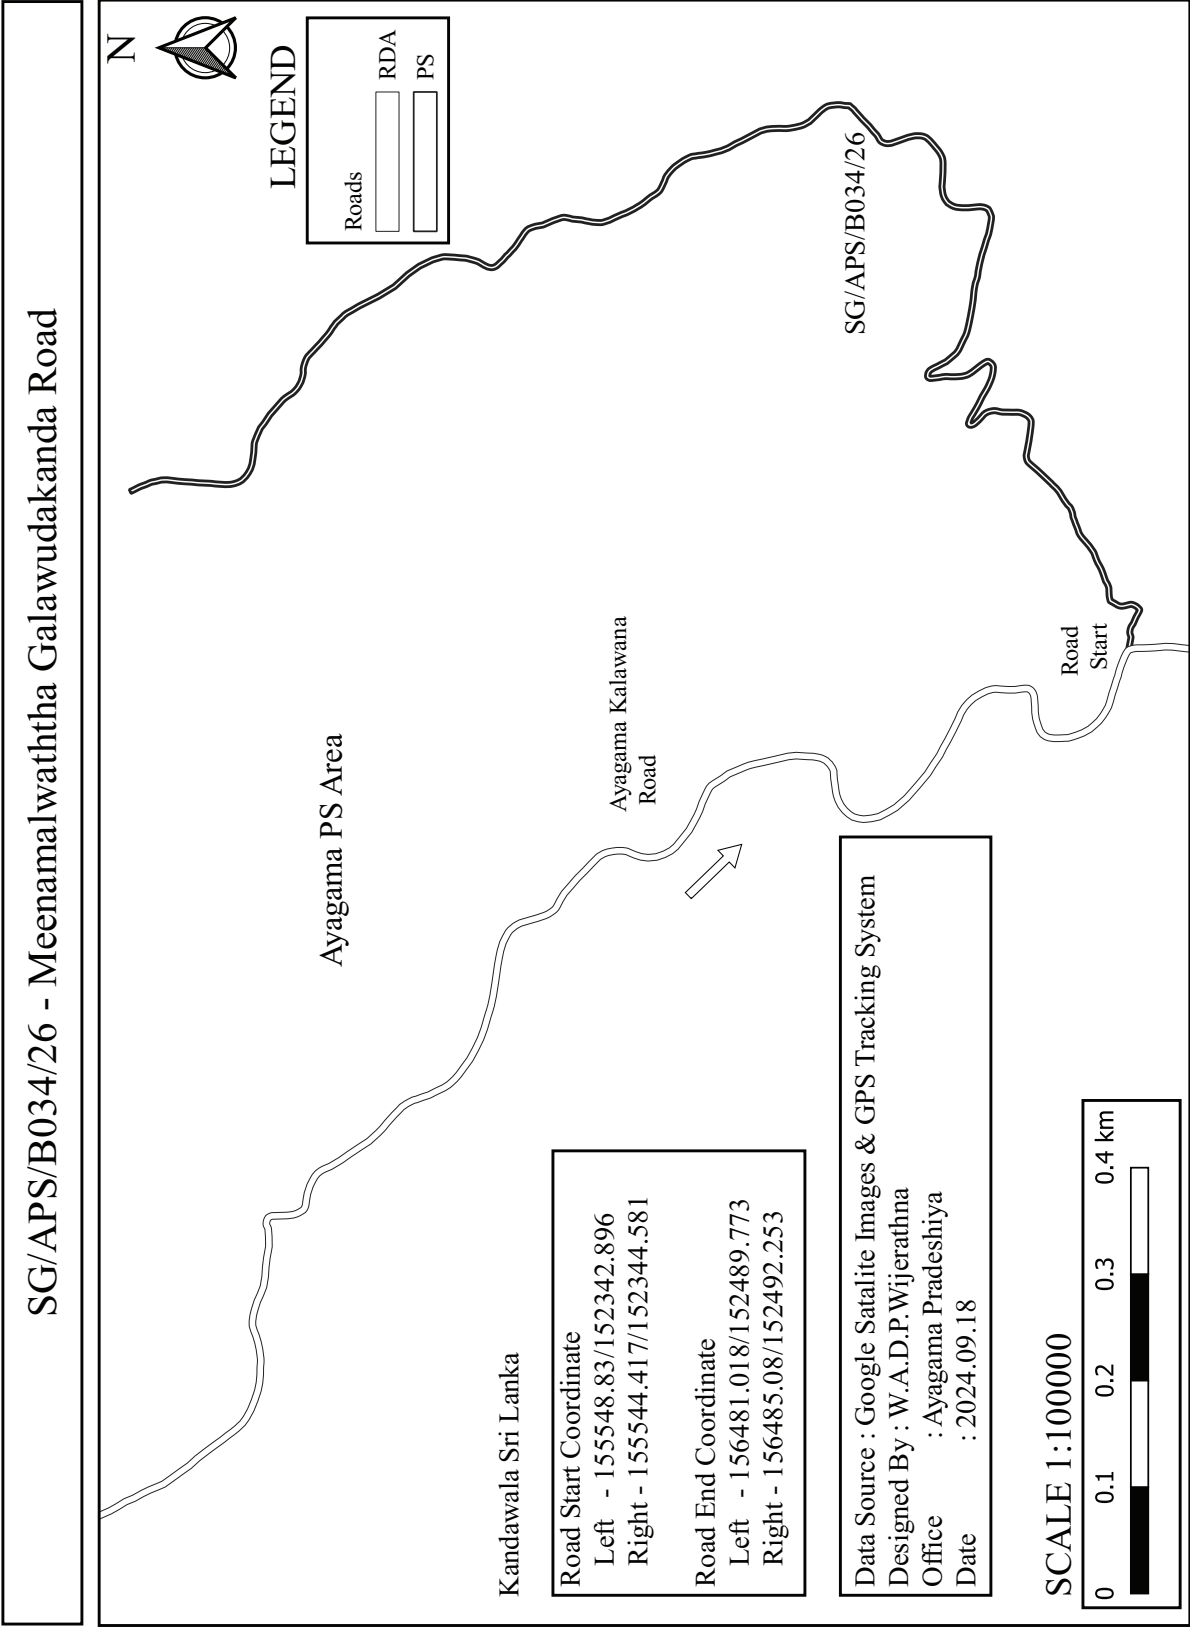

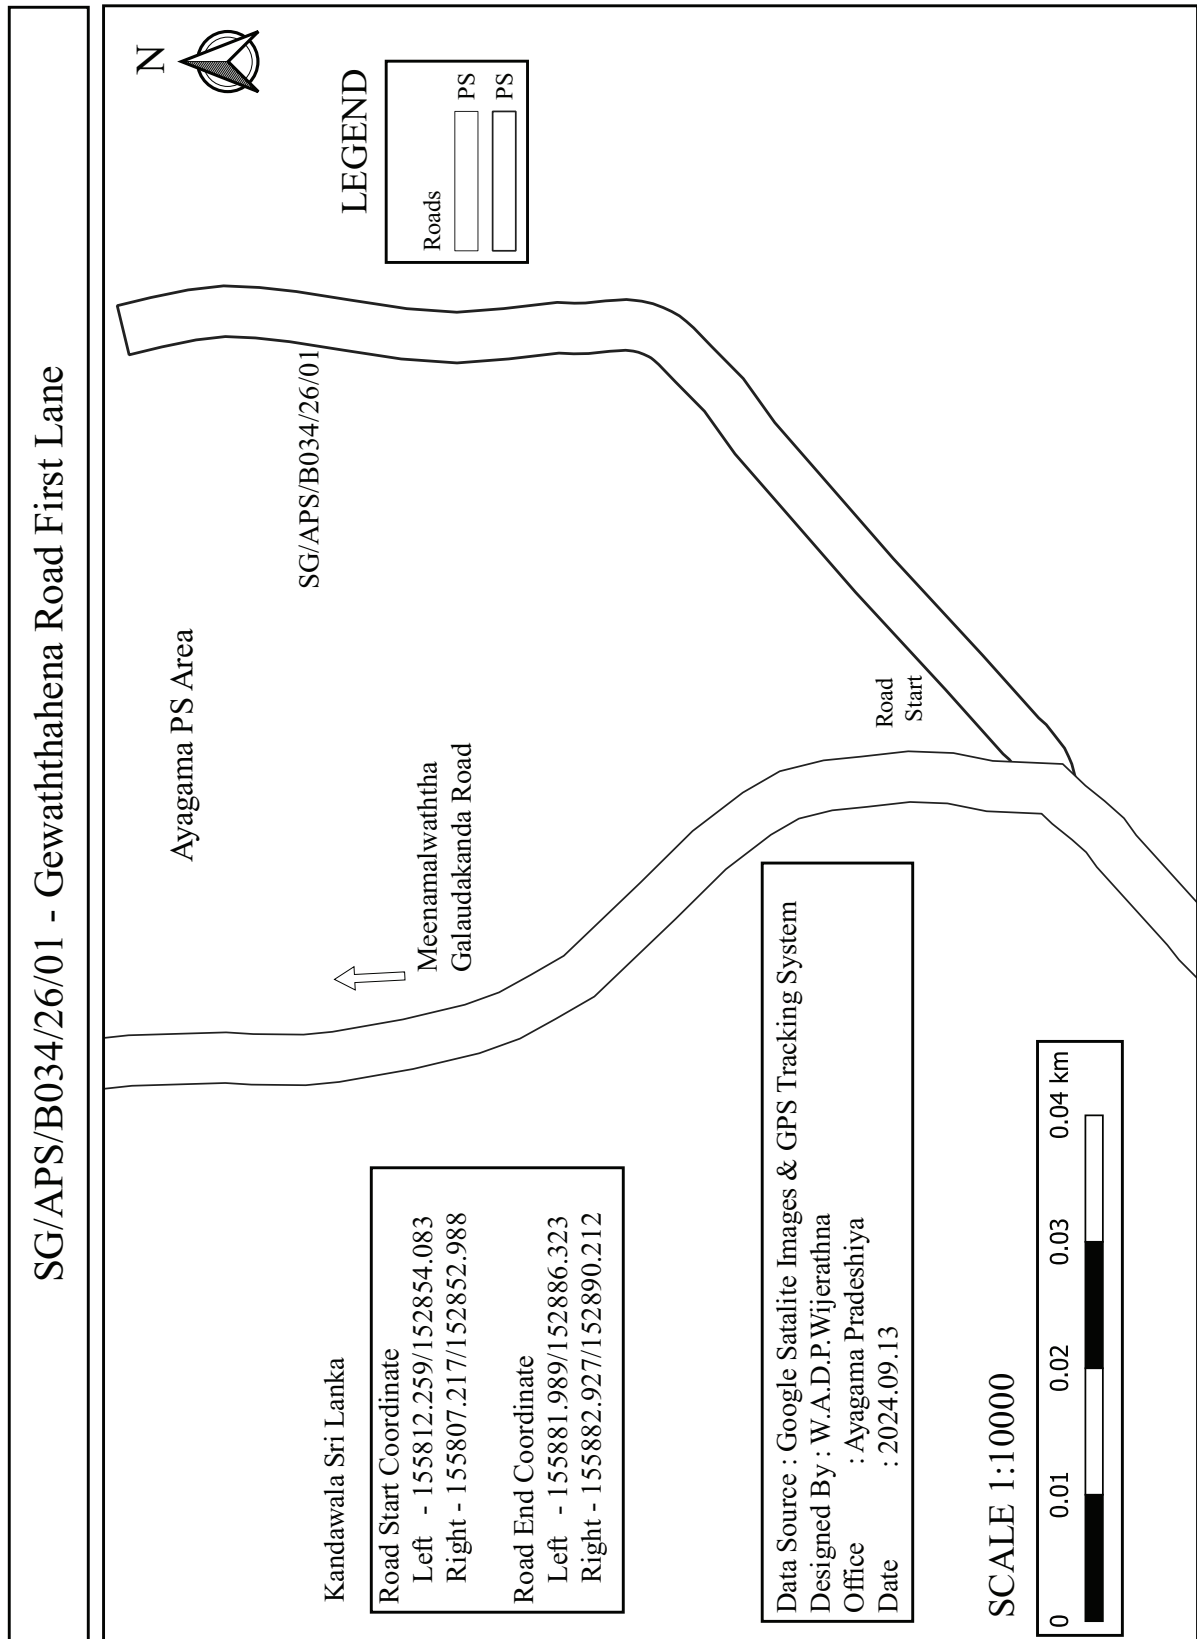


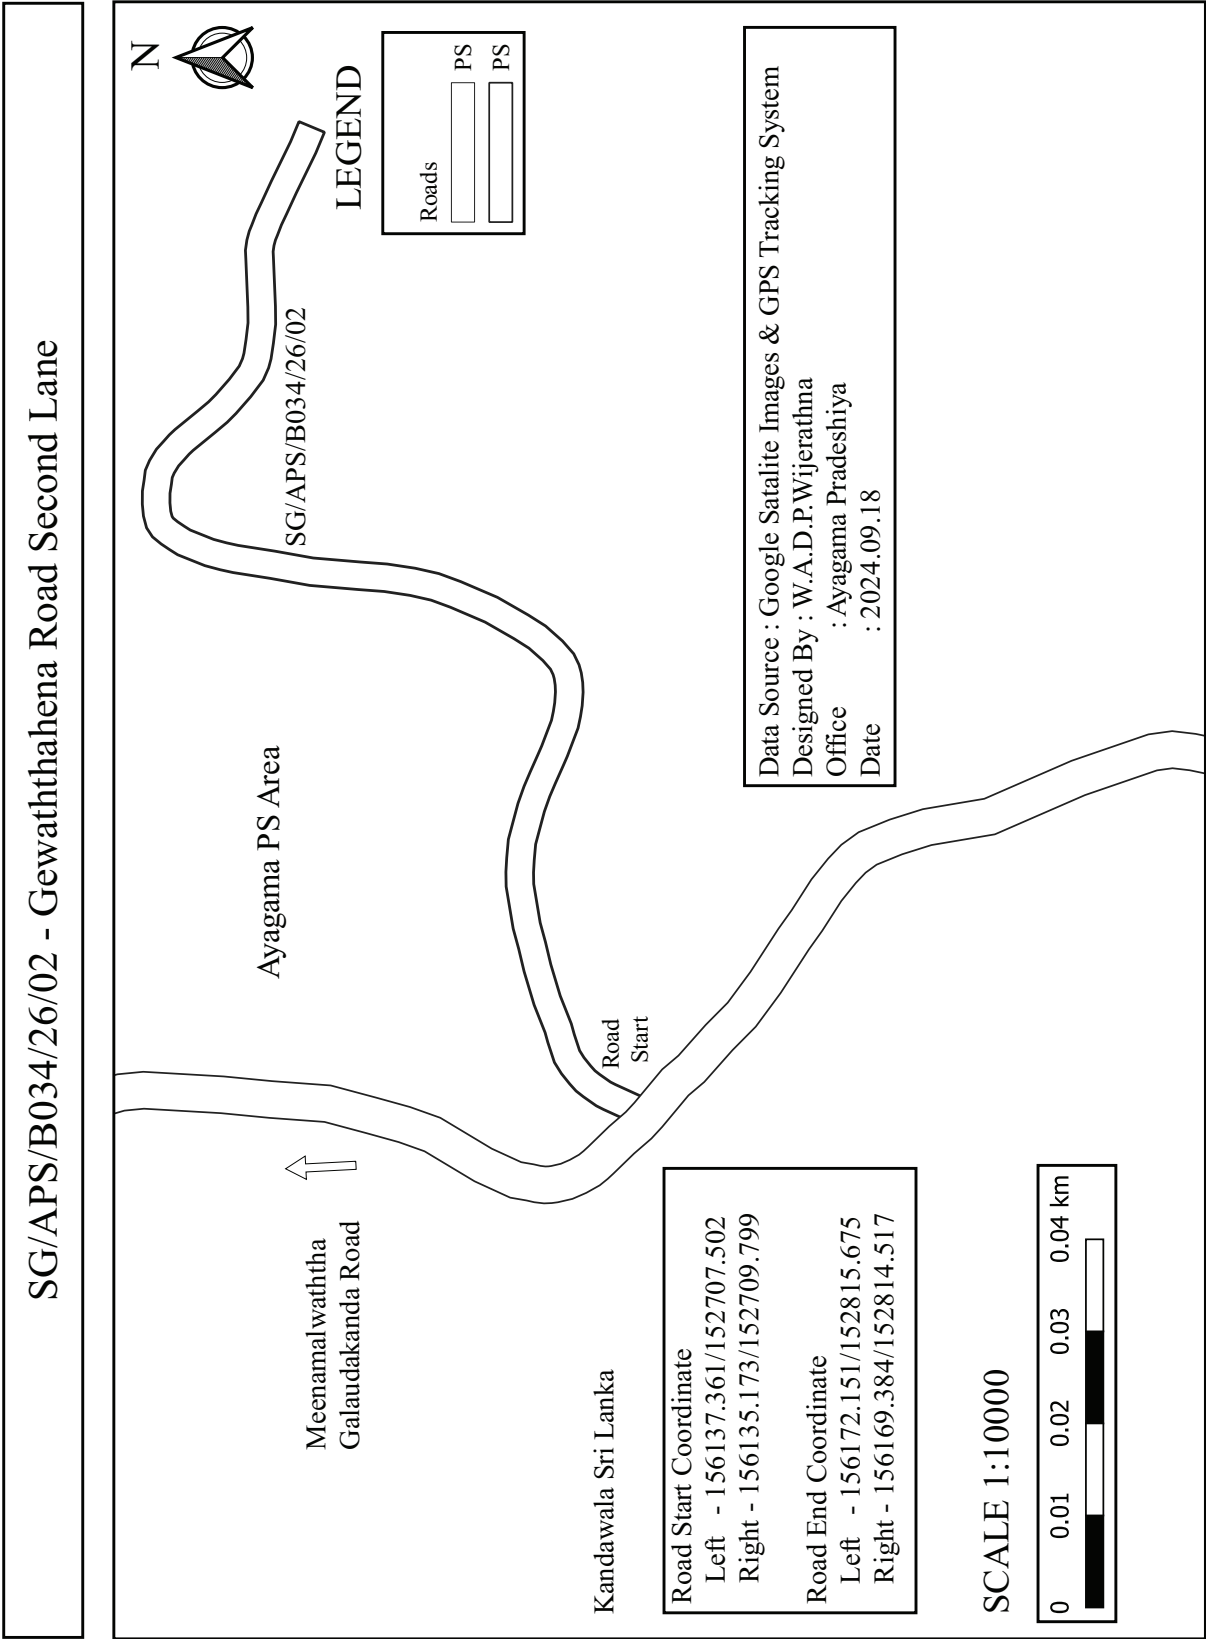

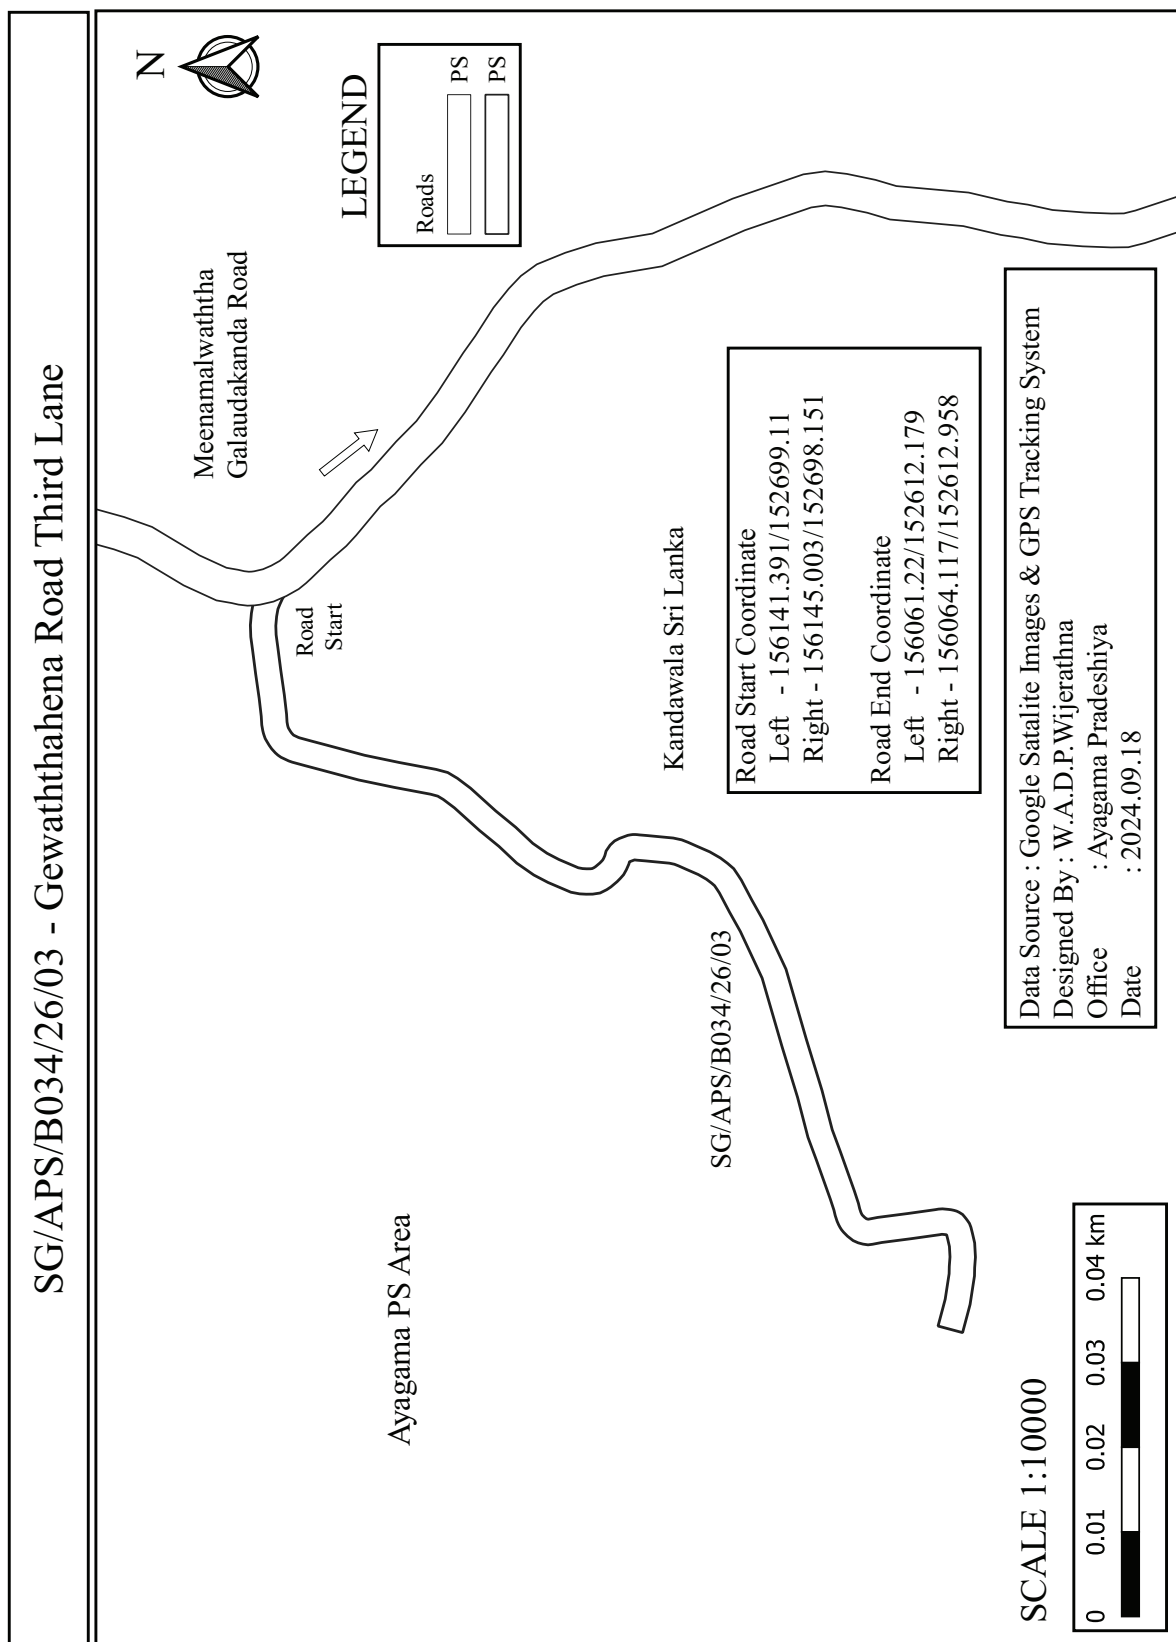


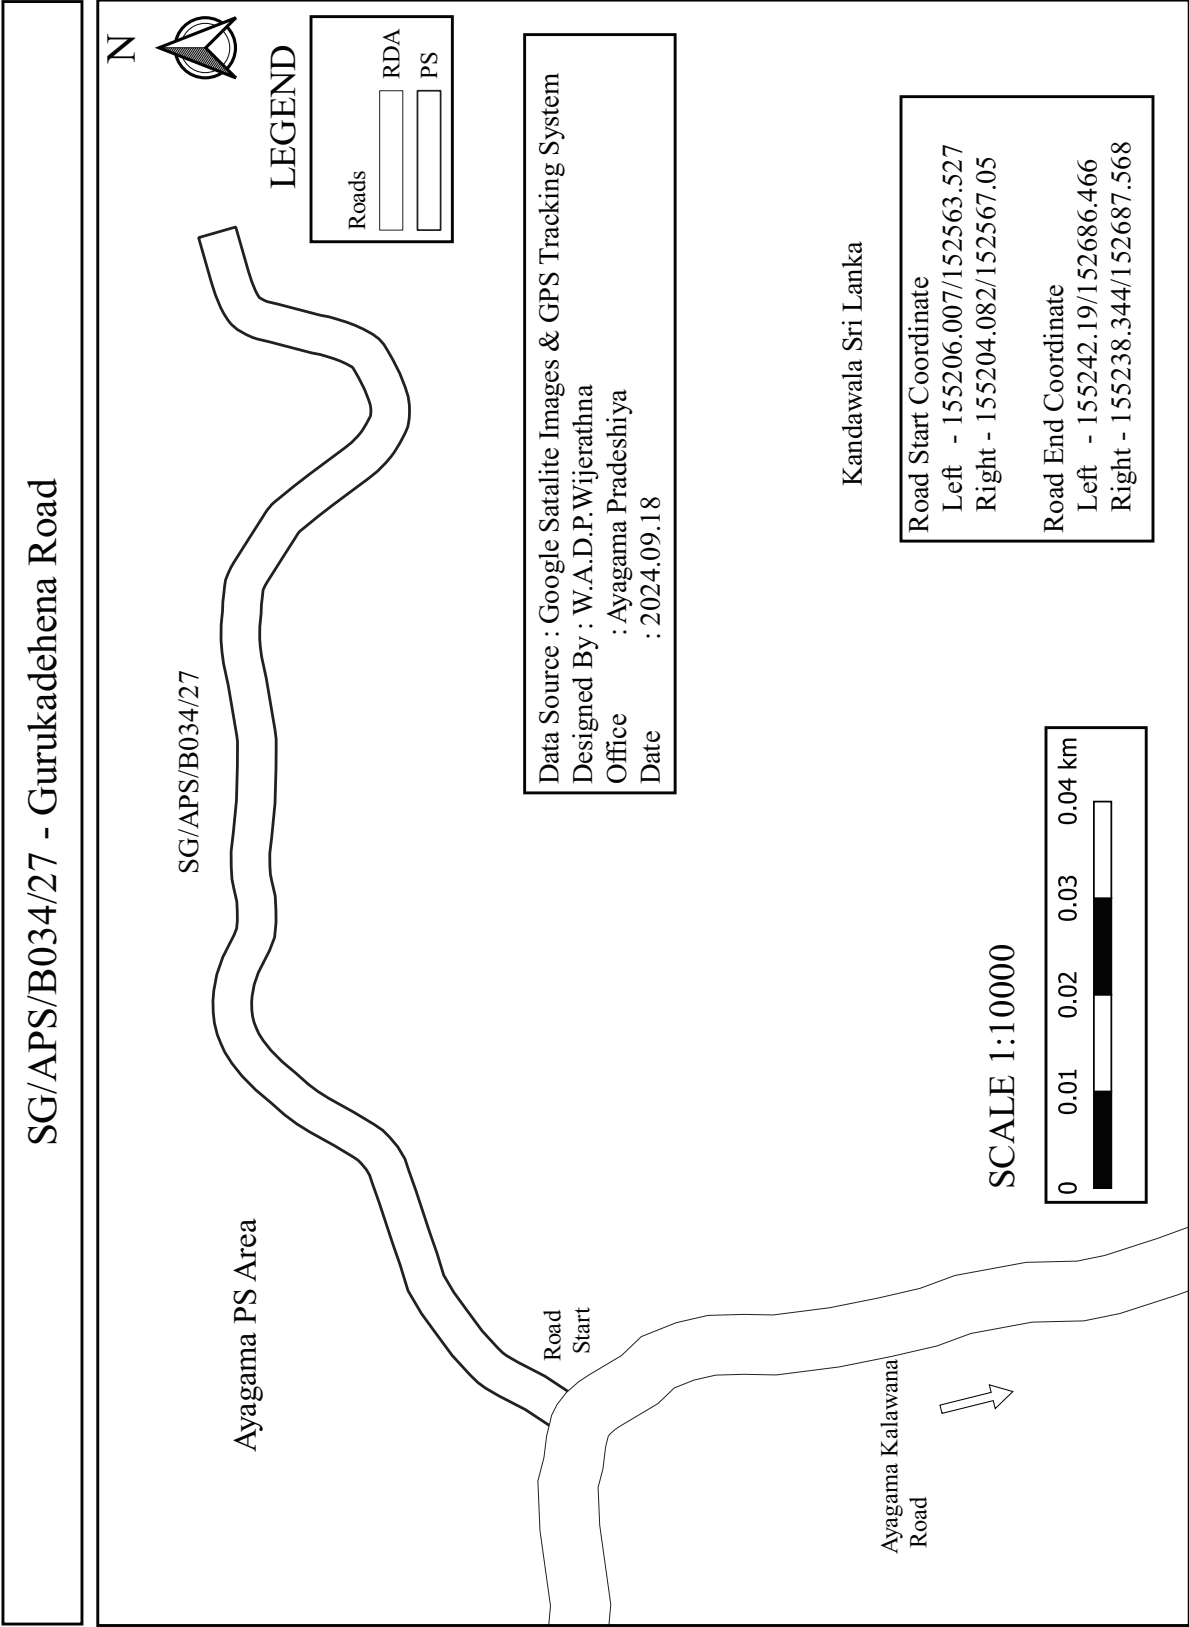





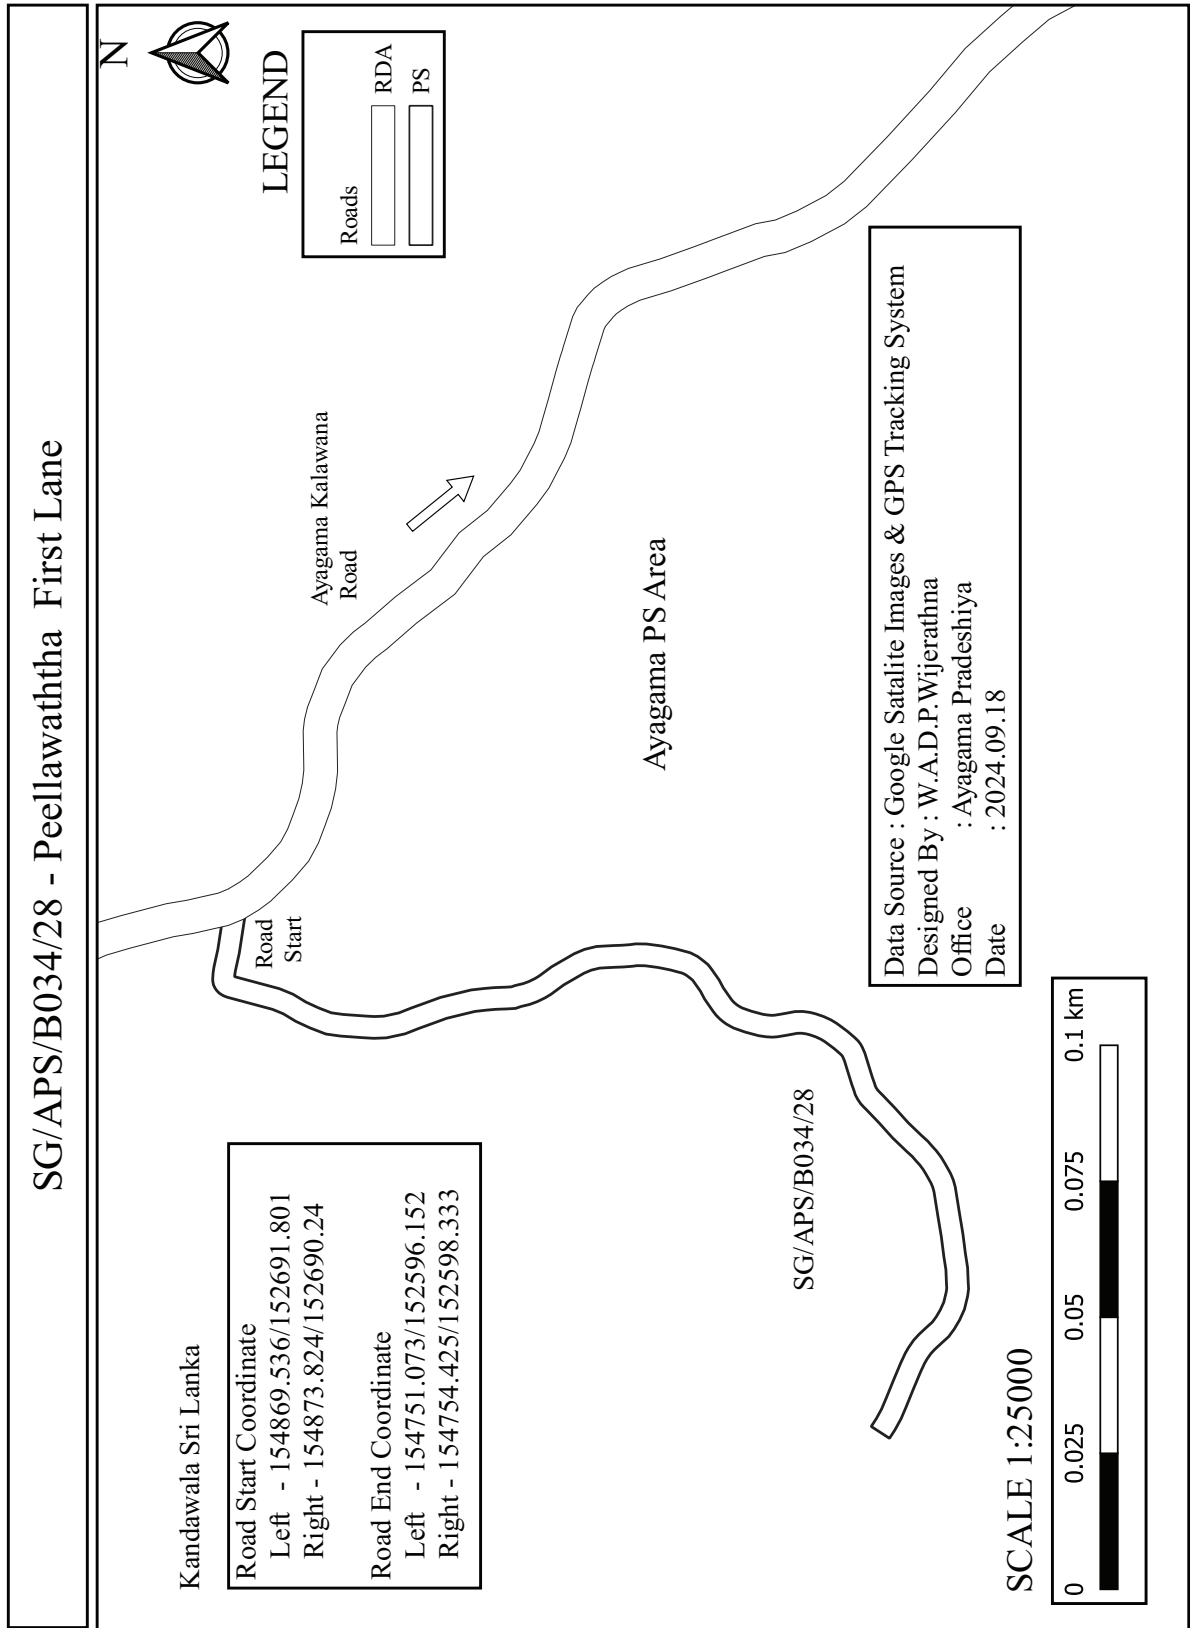



**Data Source : Google Satalite Images & GPS Tracking System**  
**Designed By : W.A.D.P. Wijerathna**  
**Office : Ayagama Pradeshiya**  
**Date : 2024.09.18**

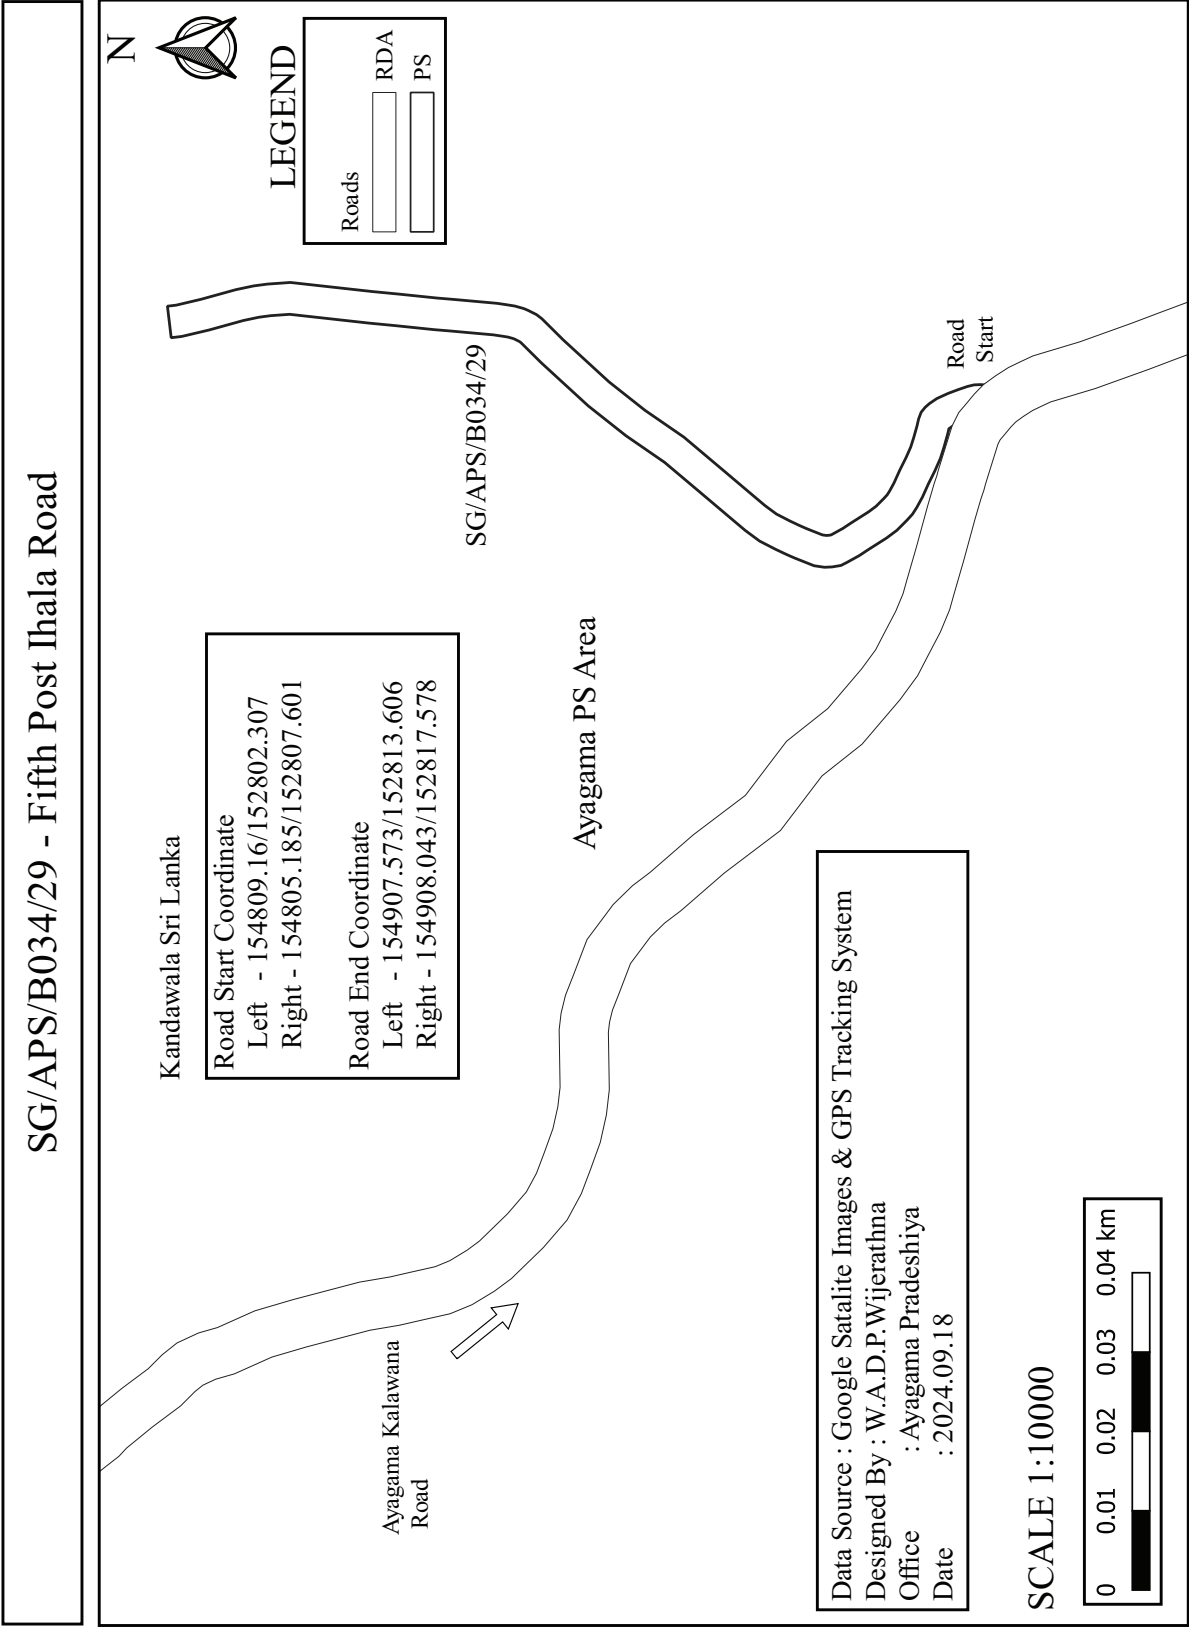


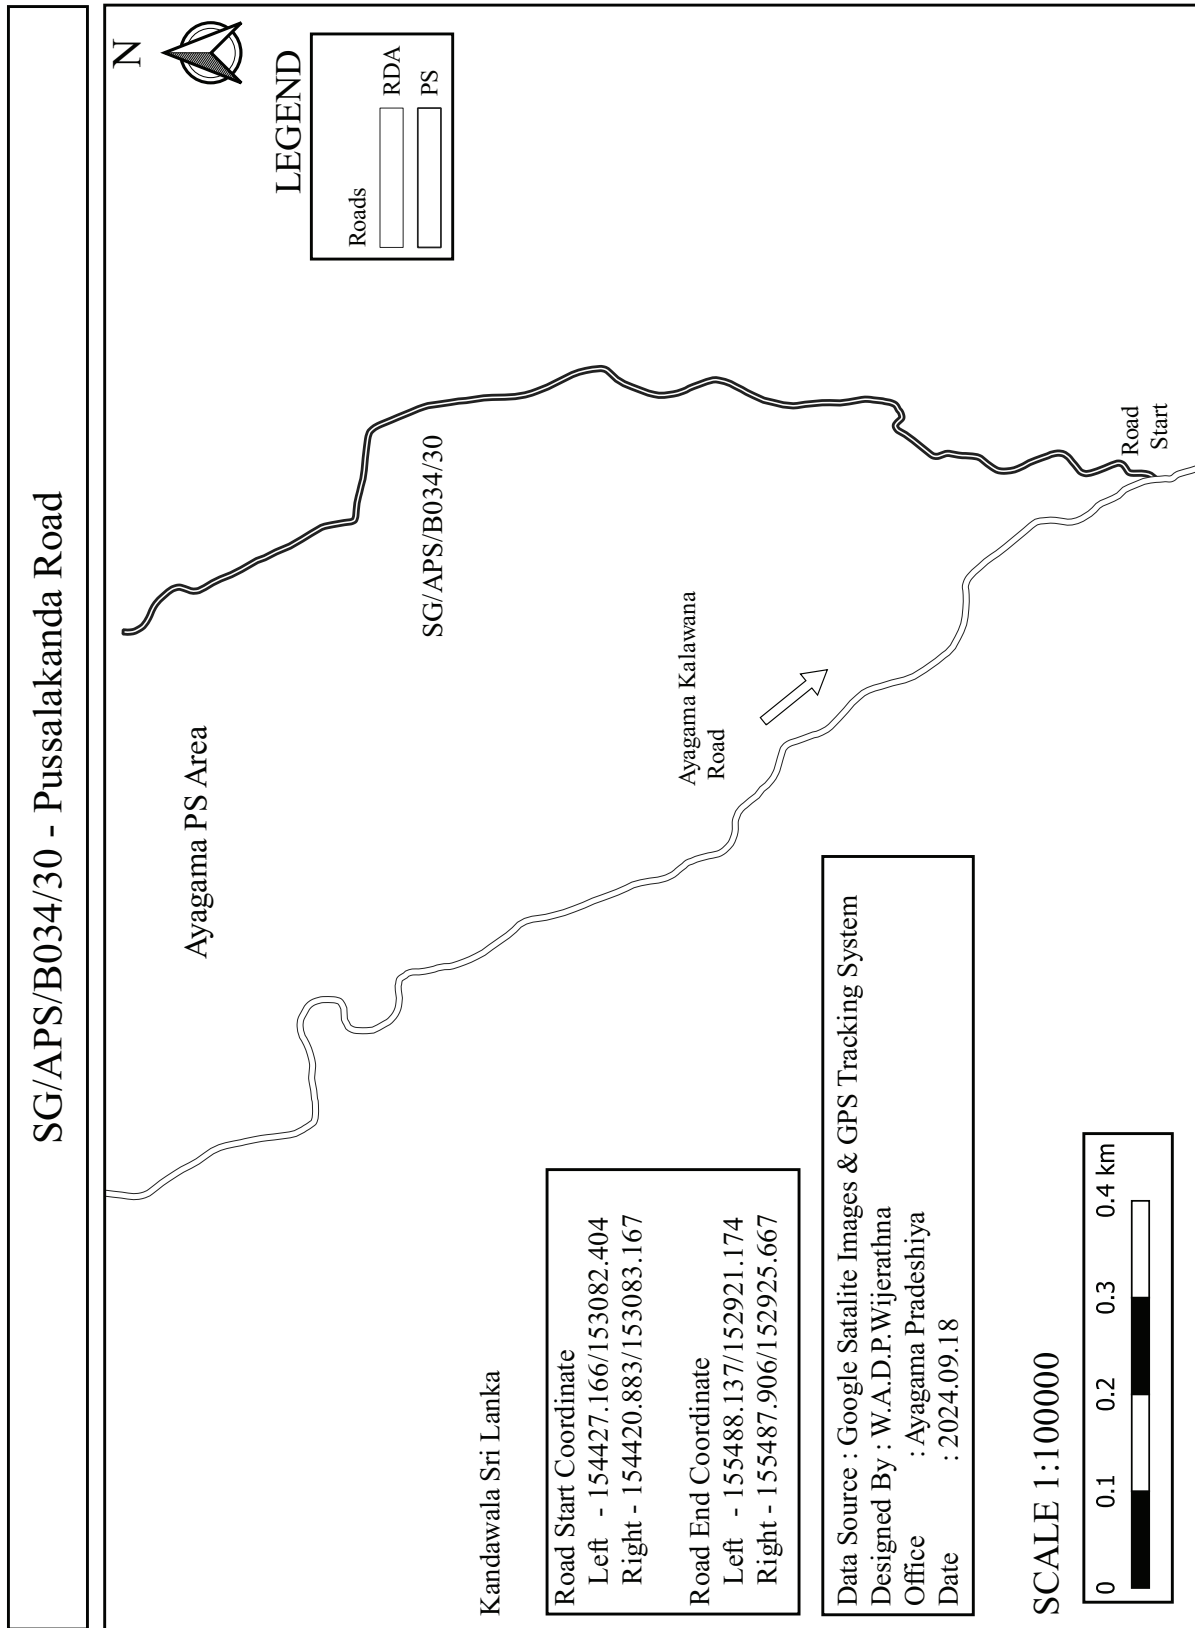


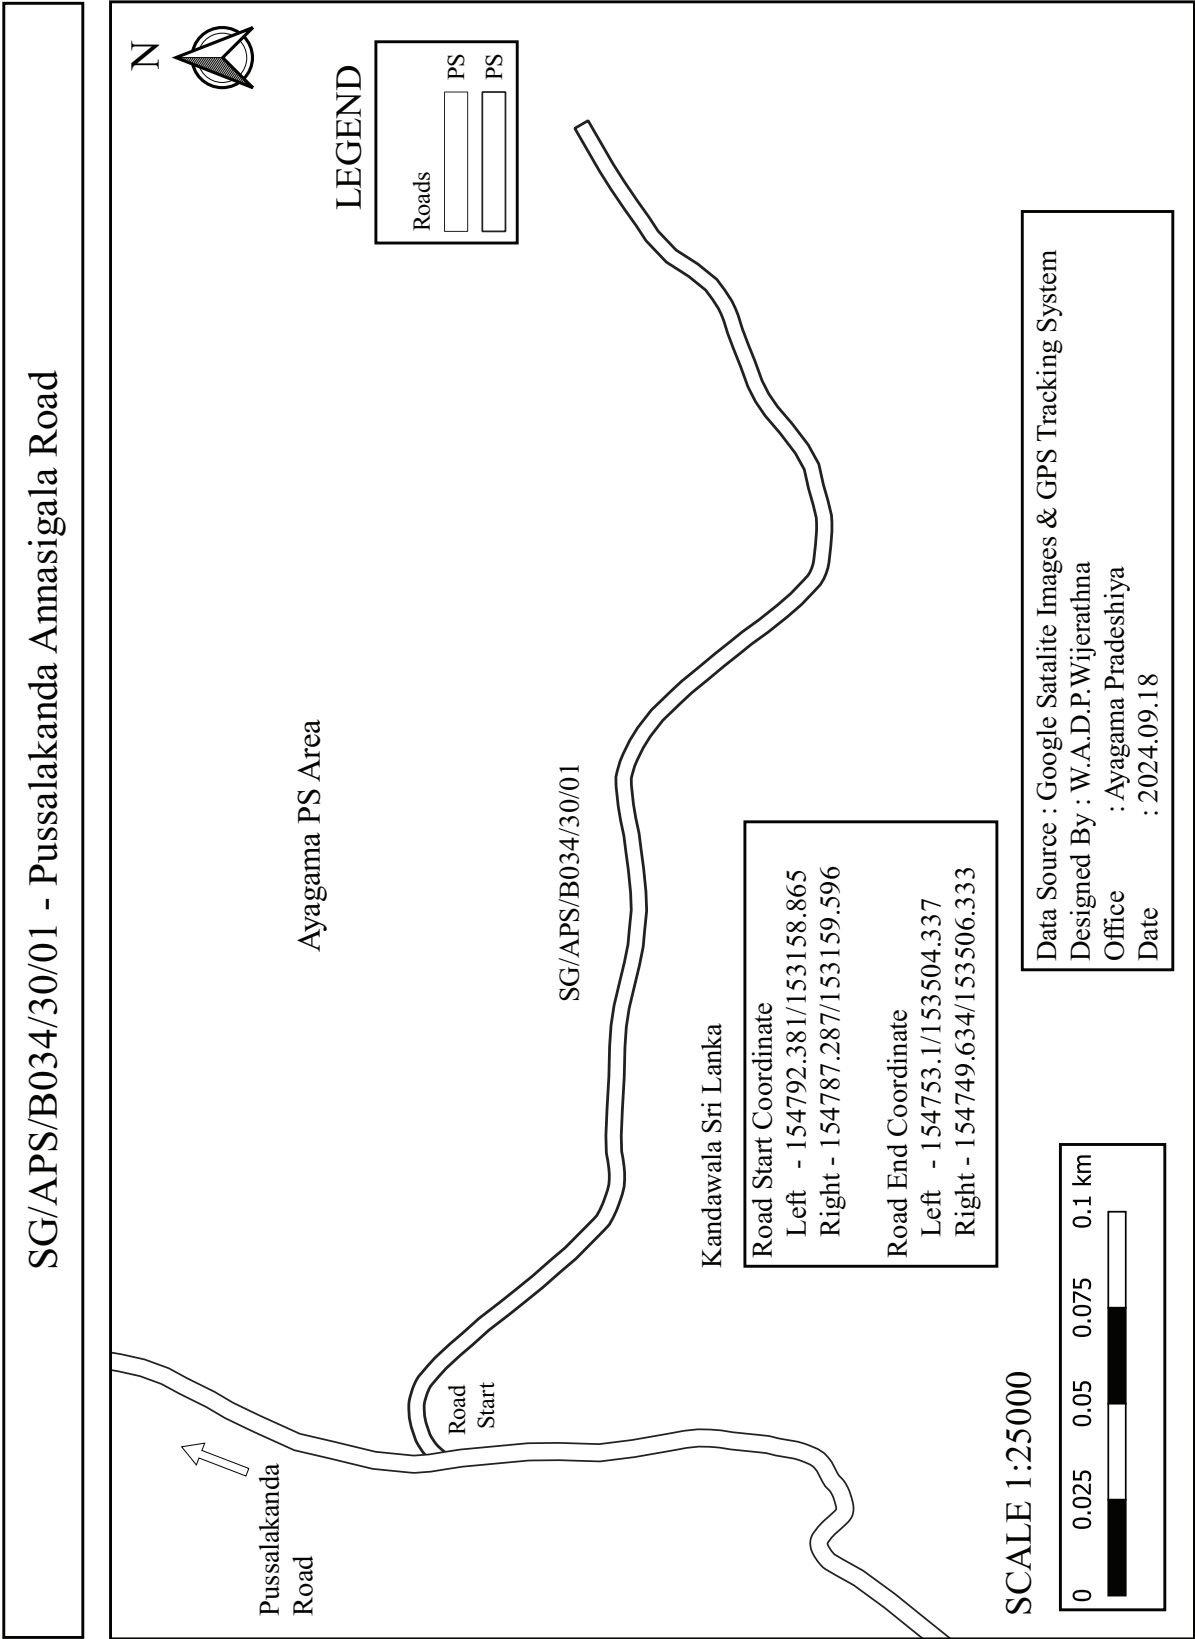

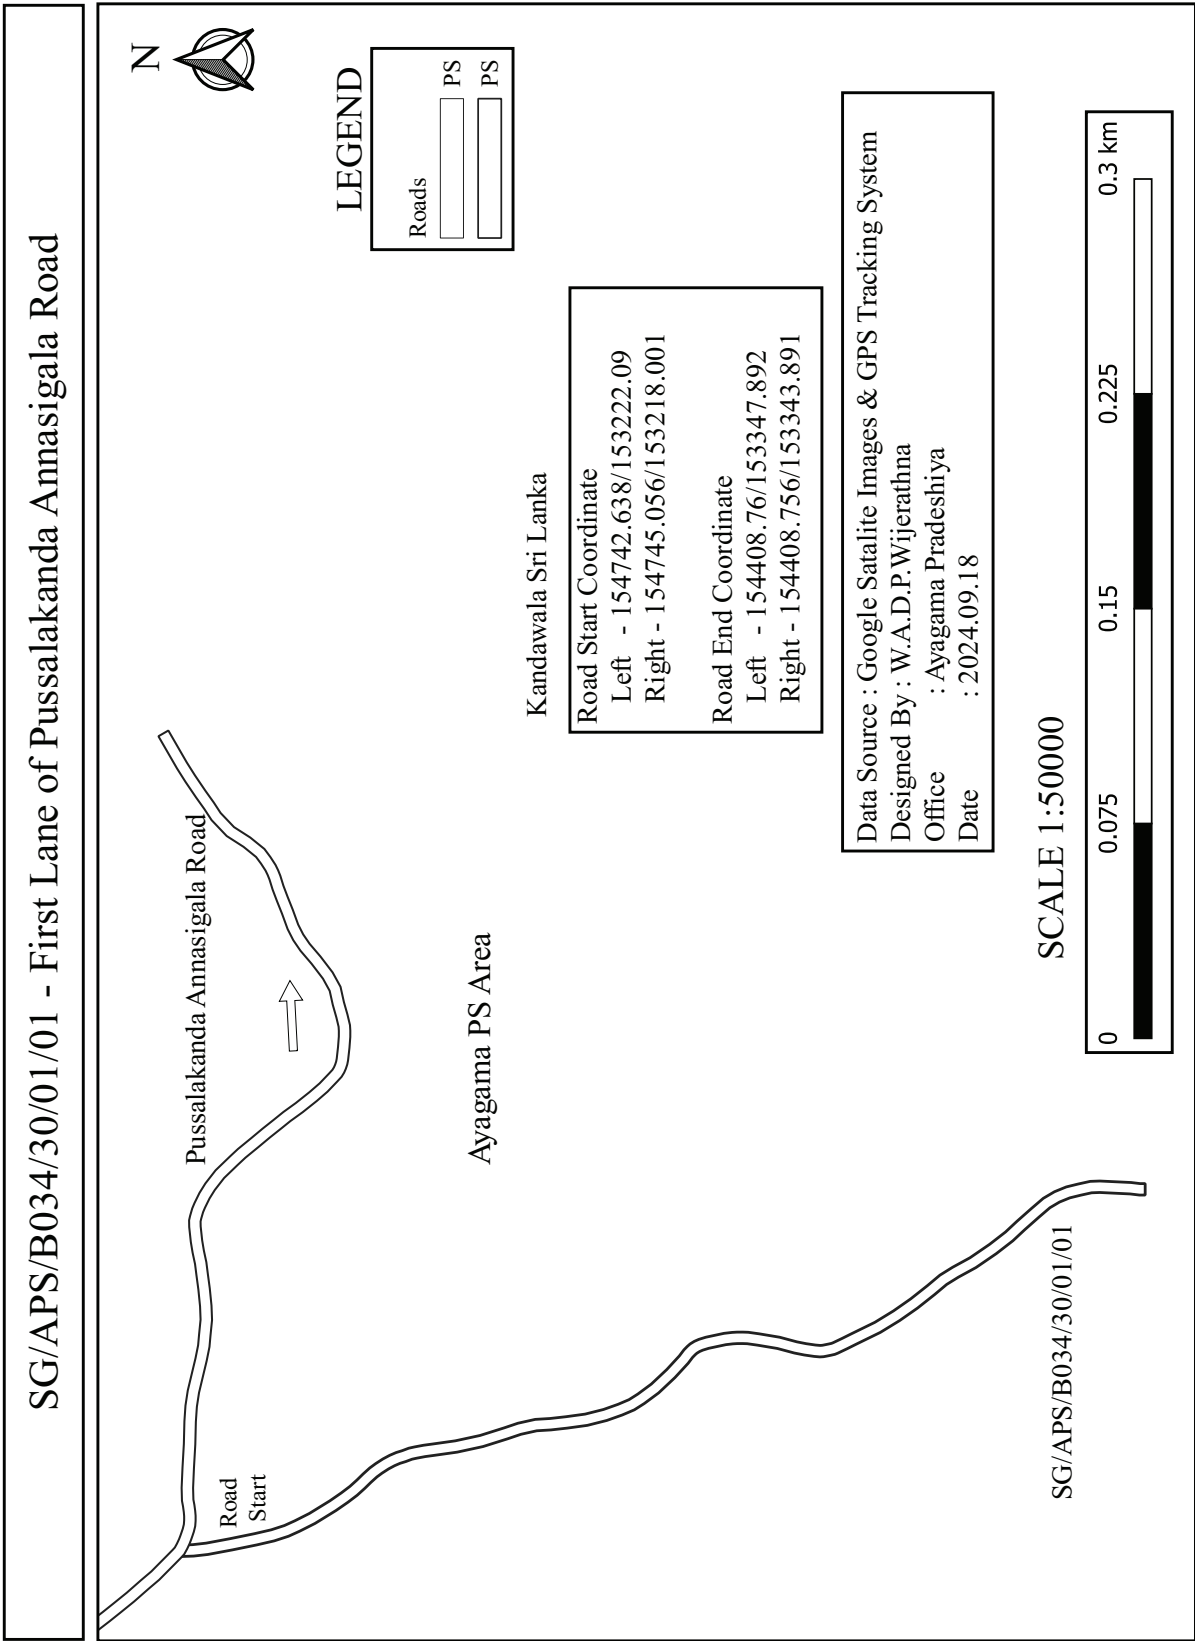


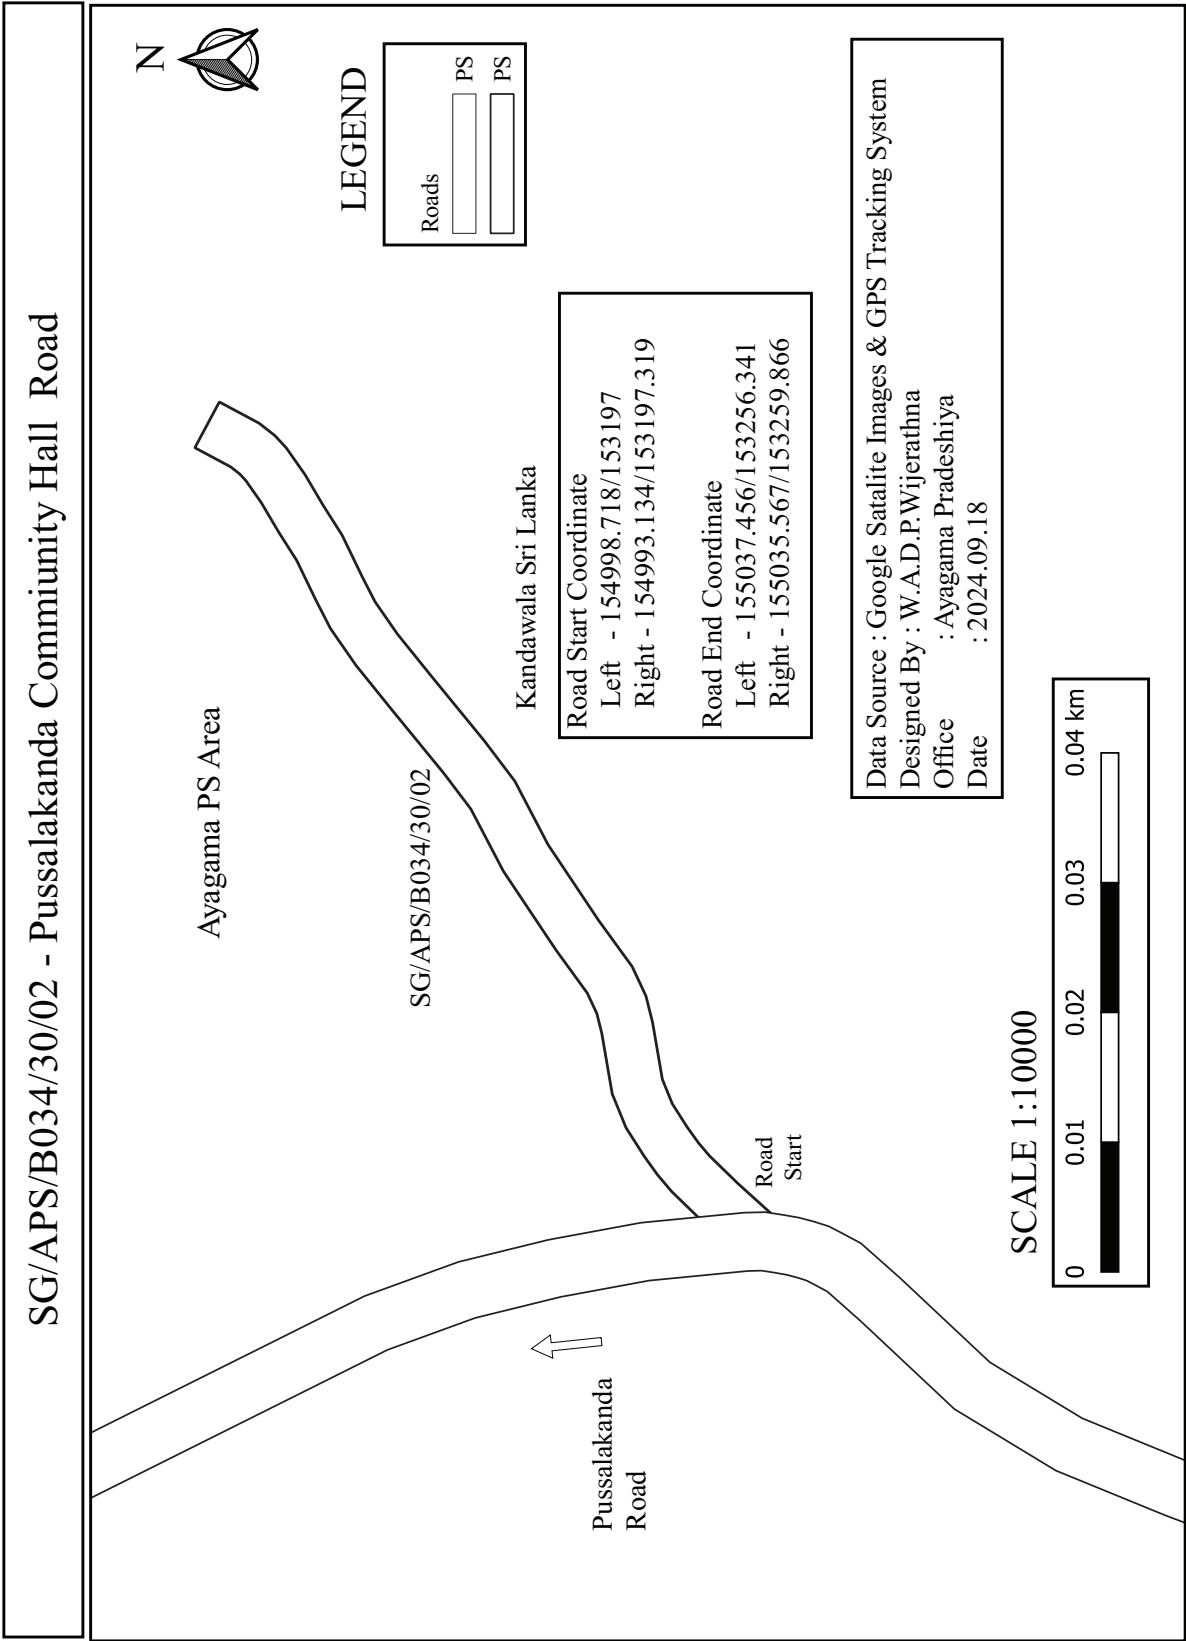


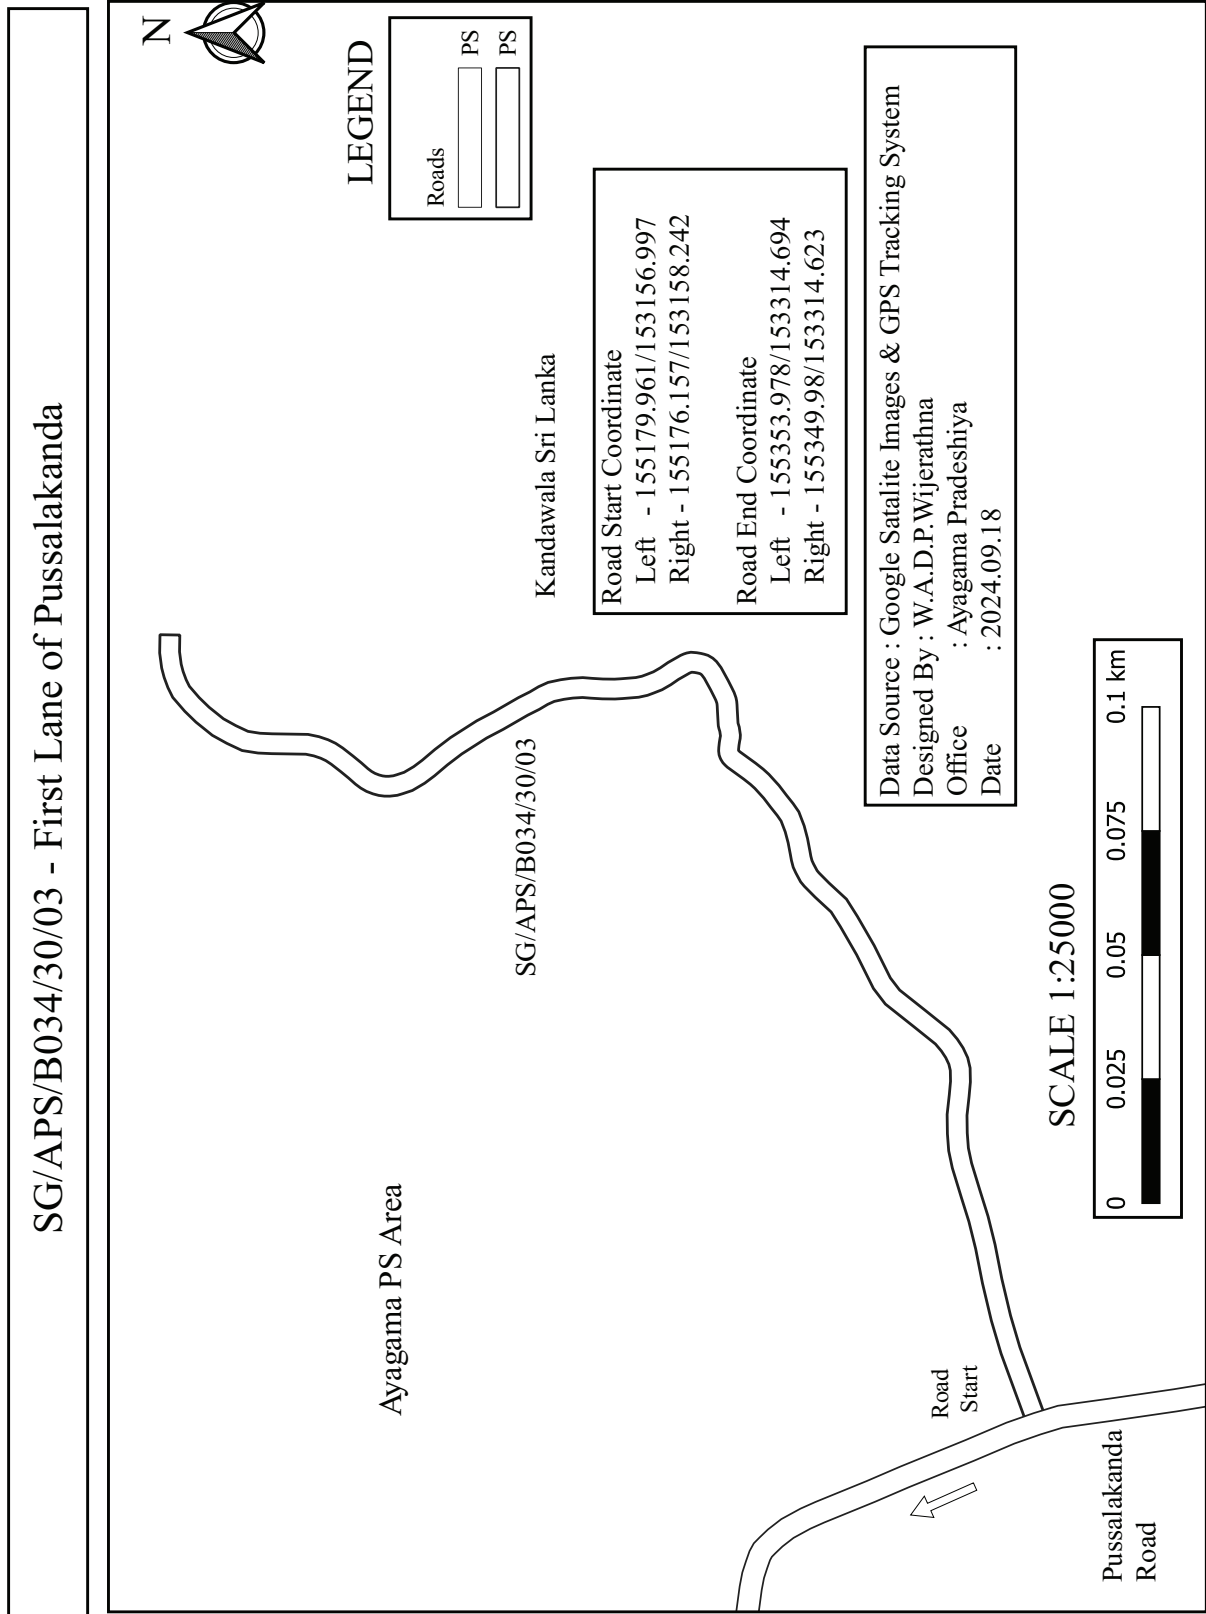


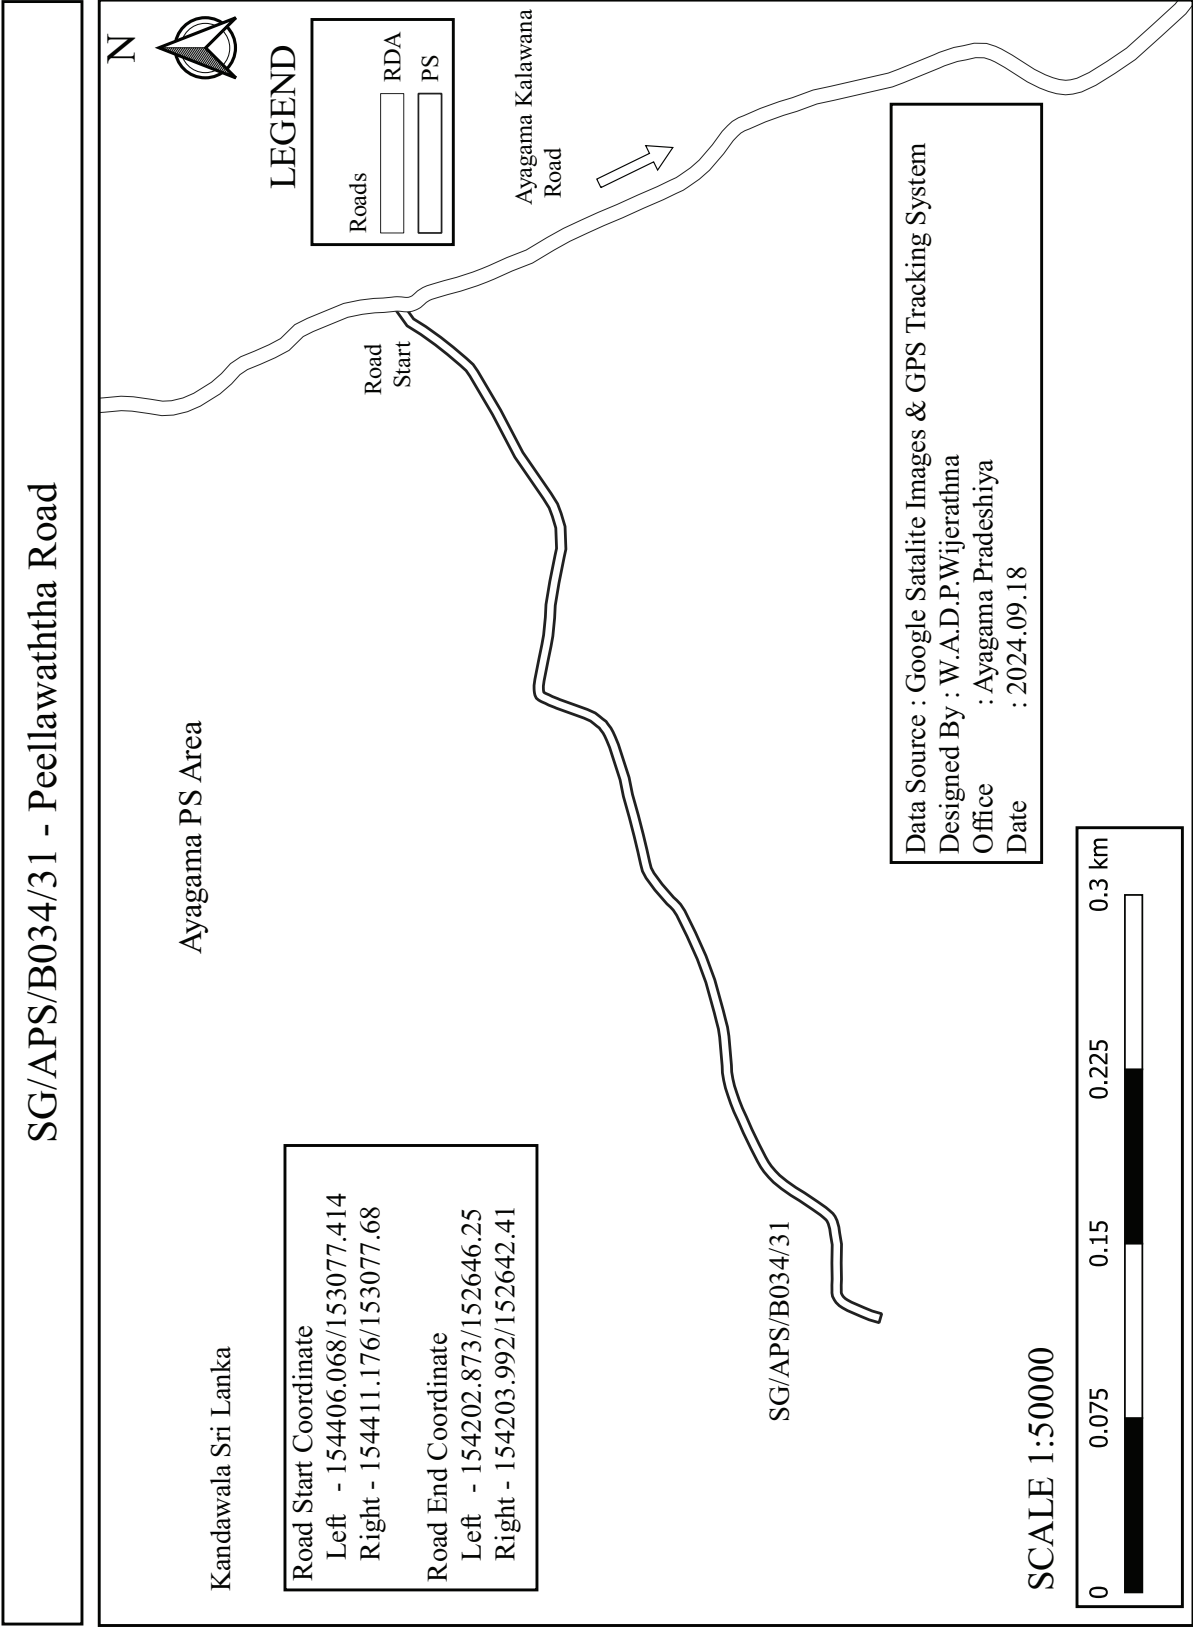





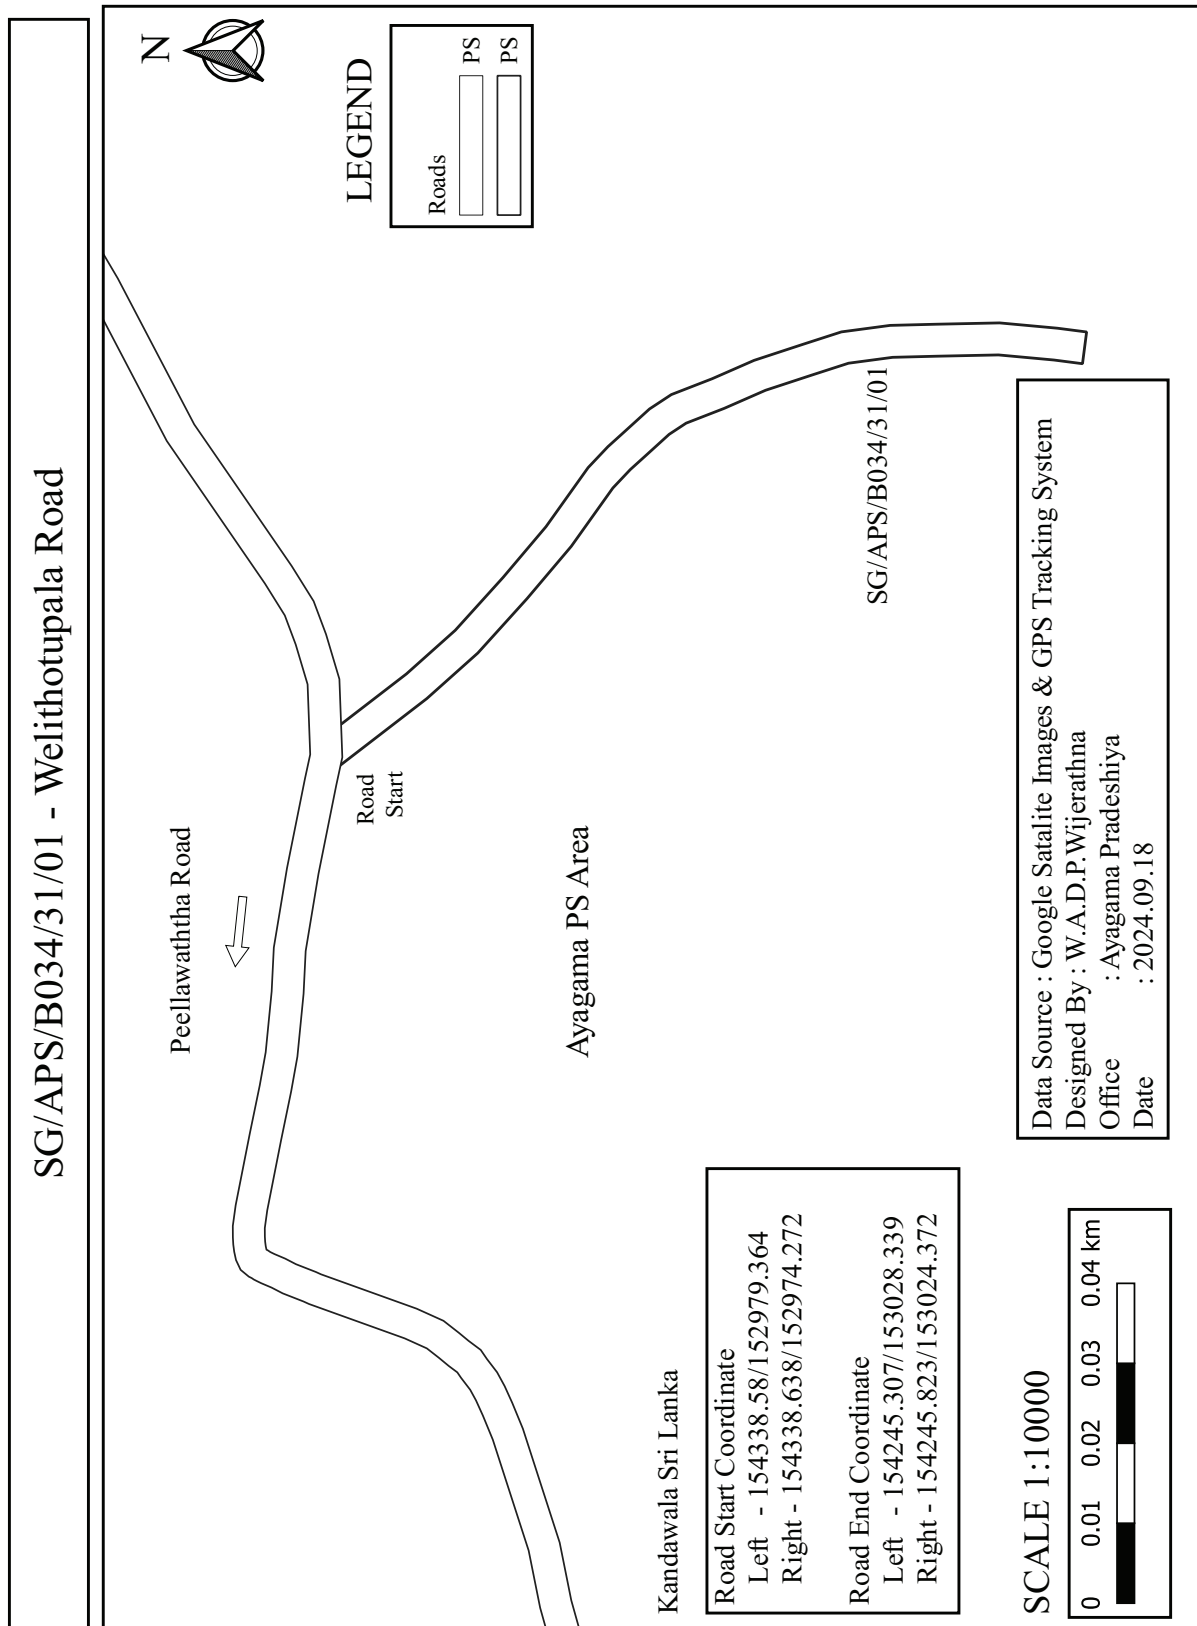


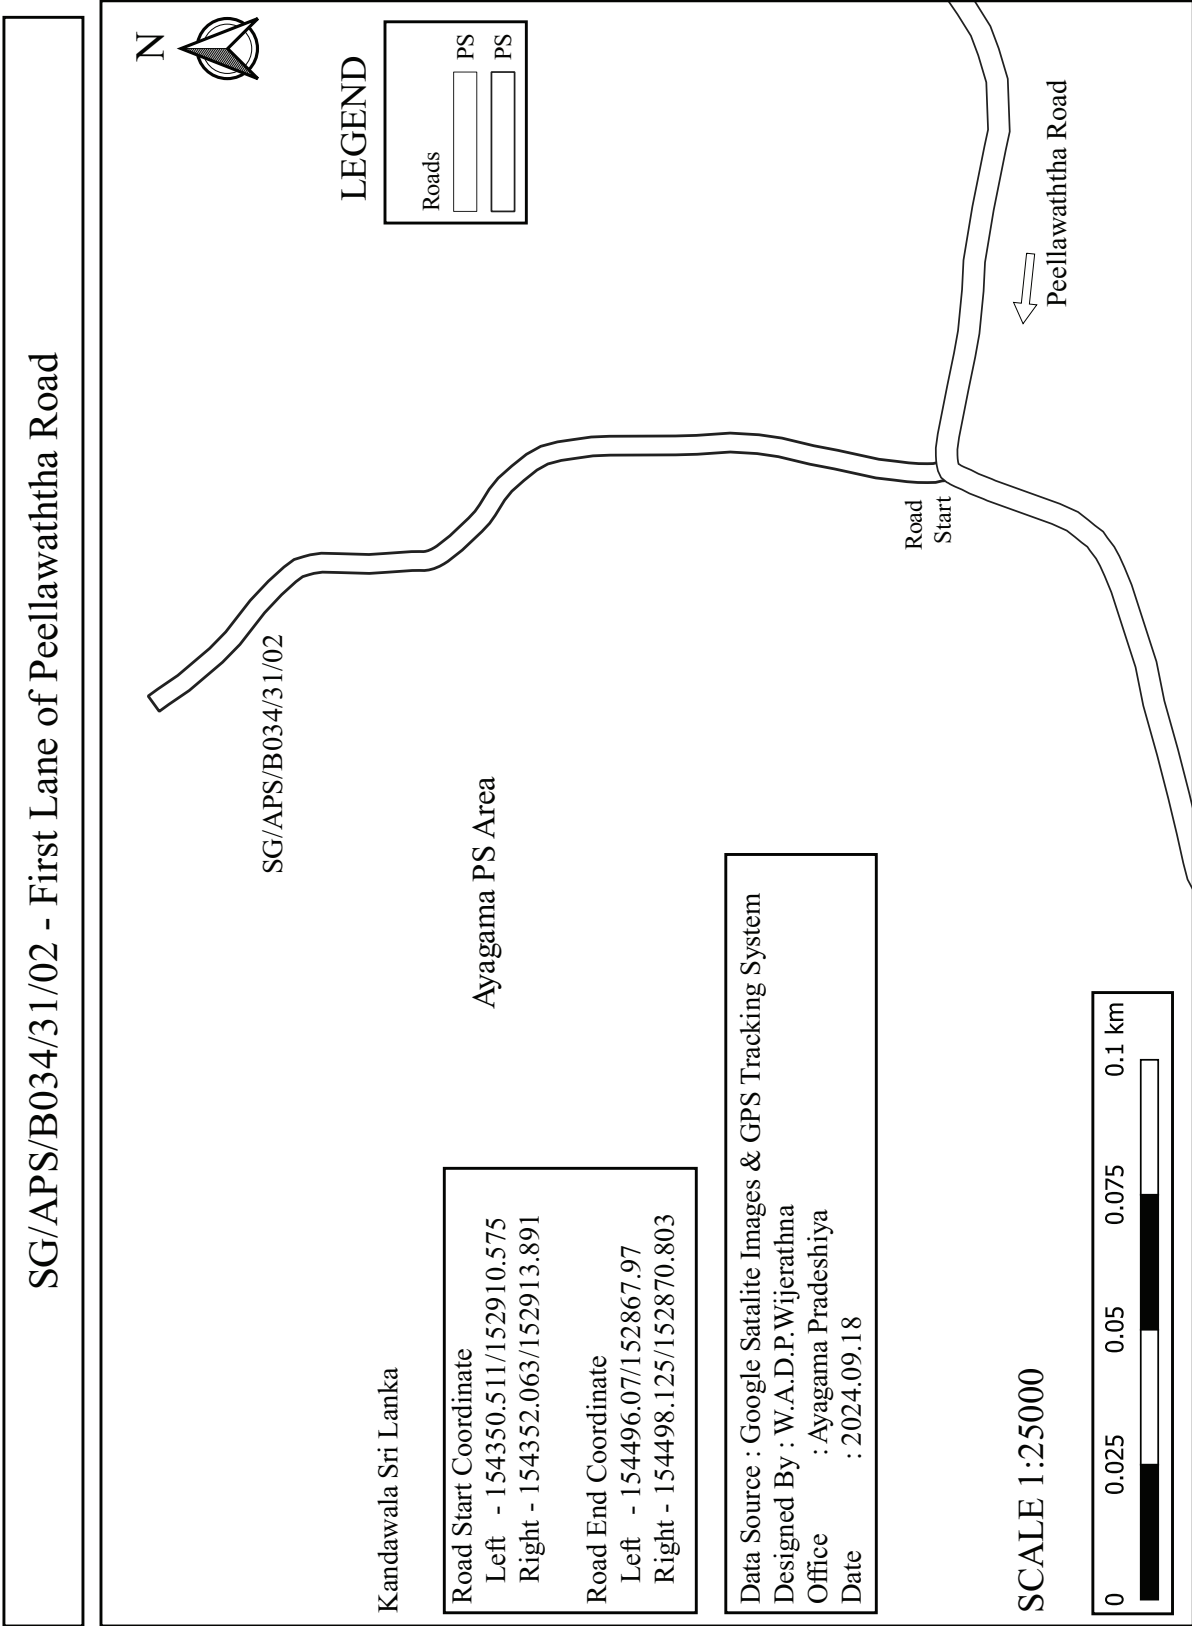


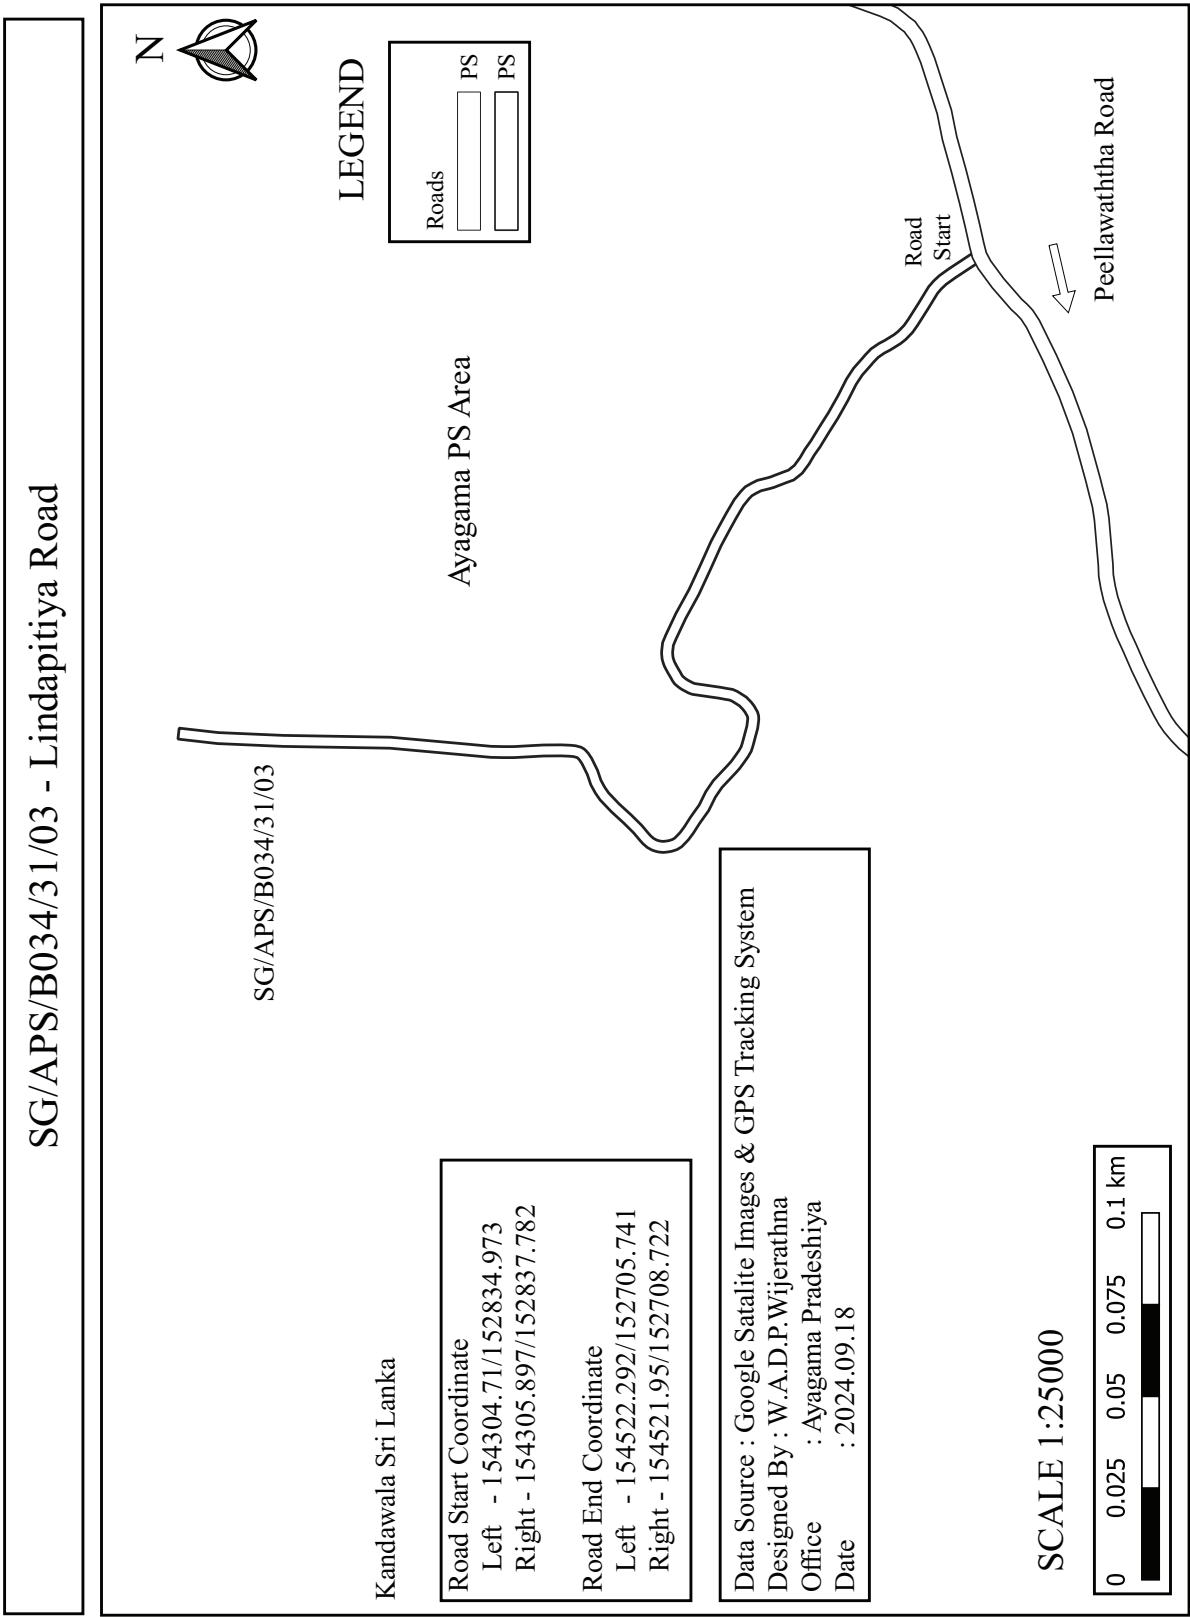


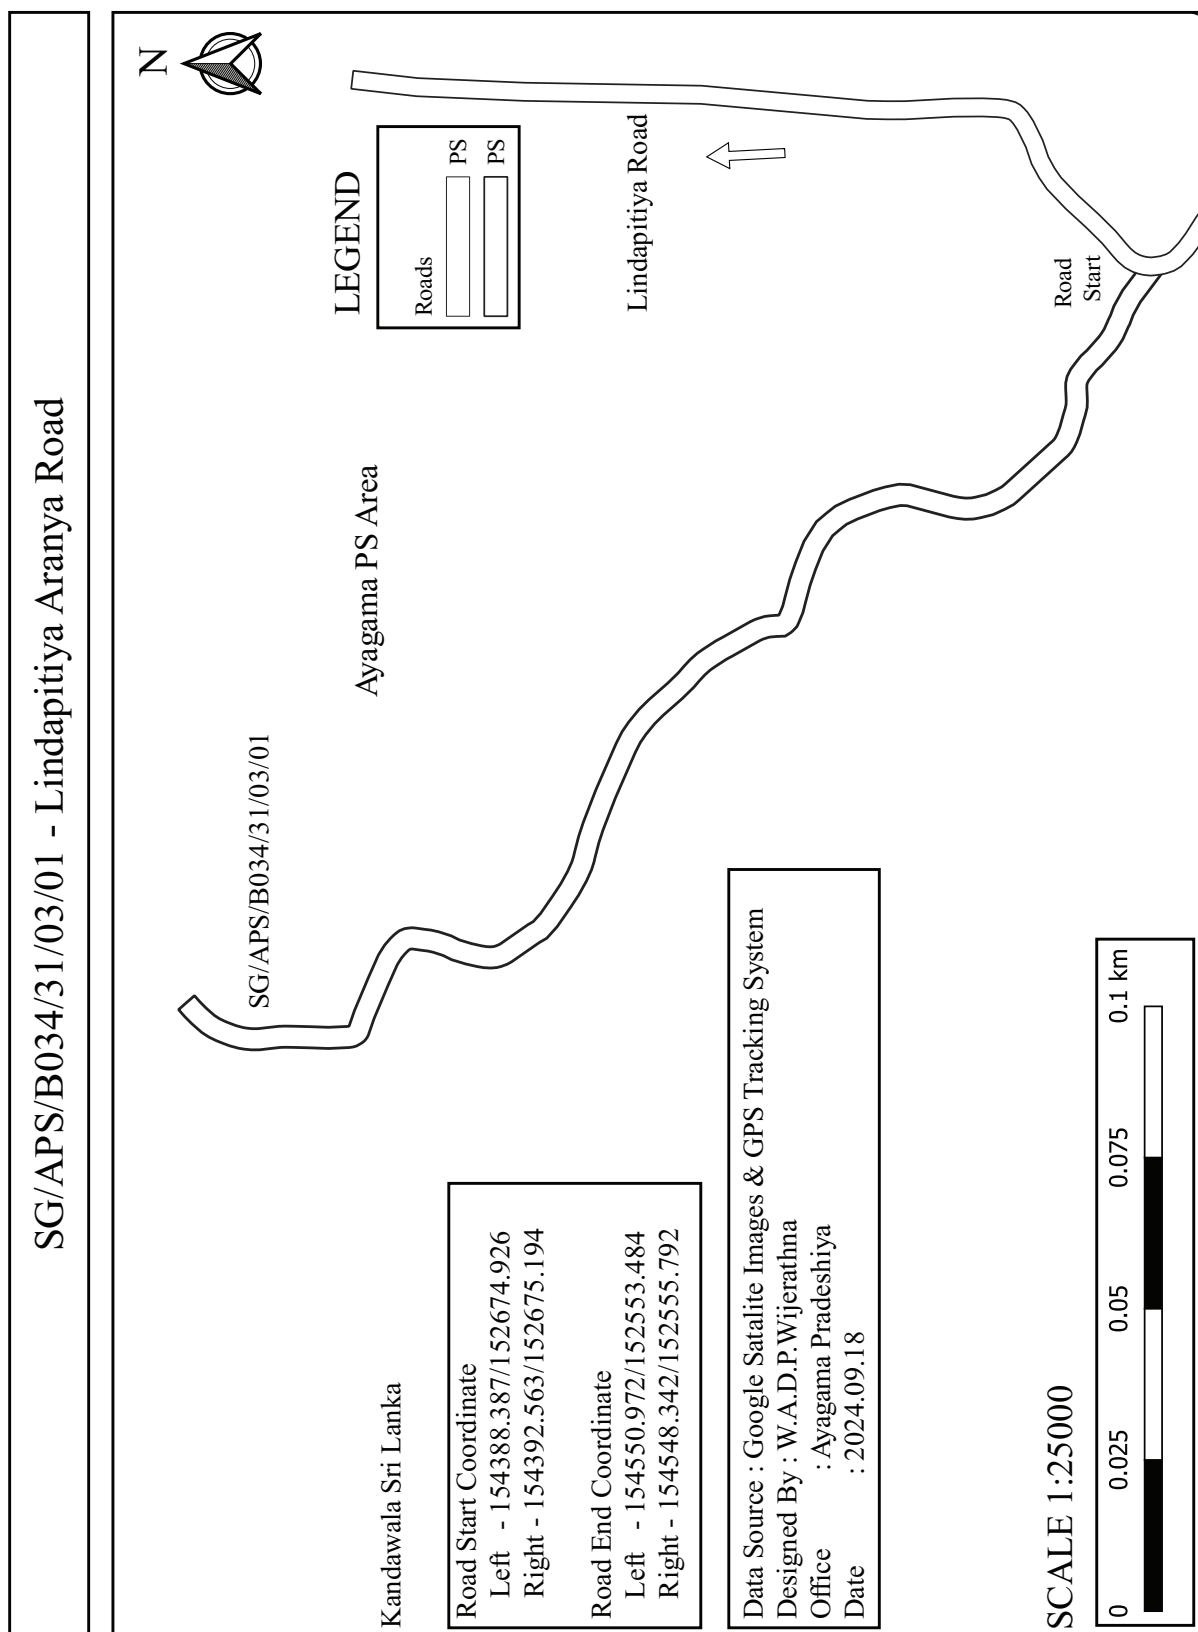

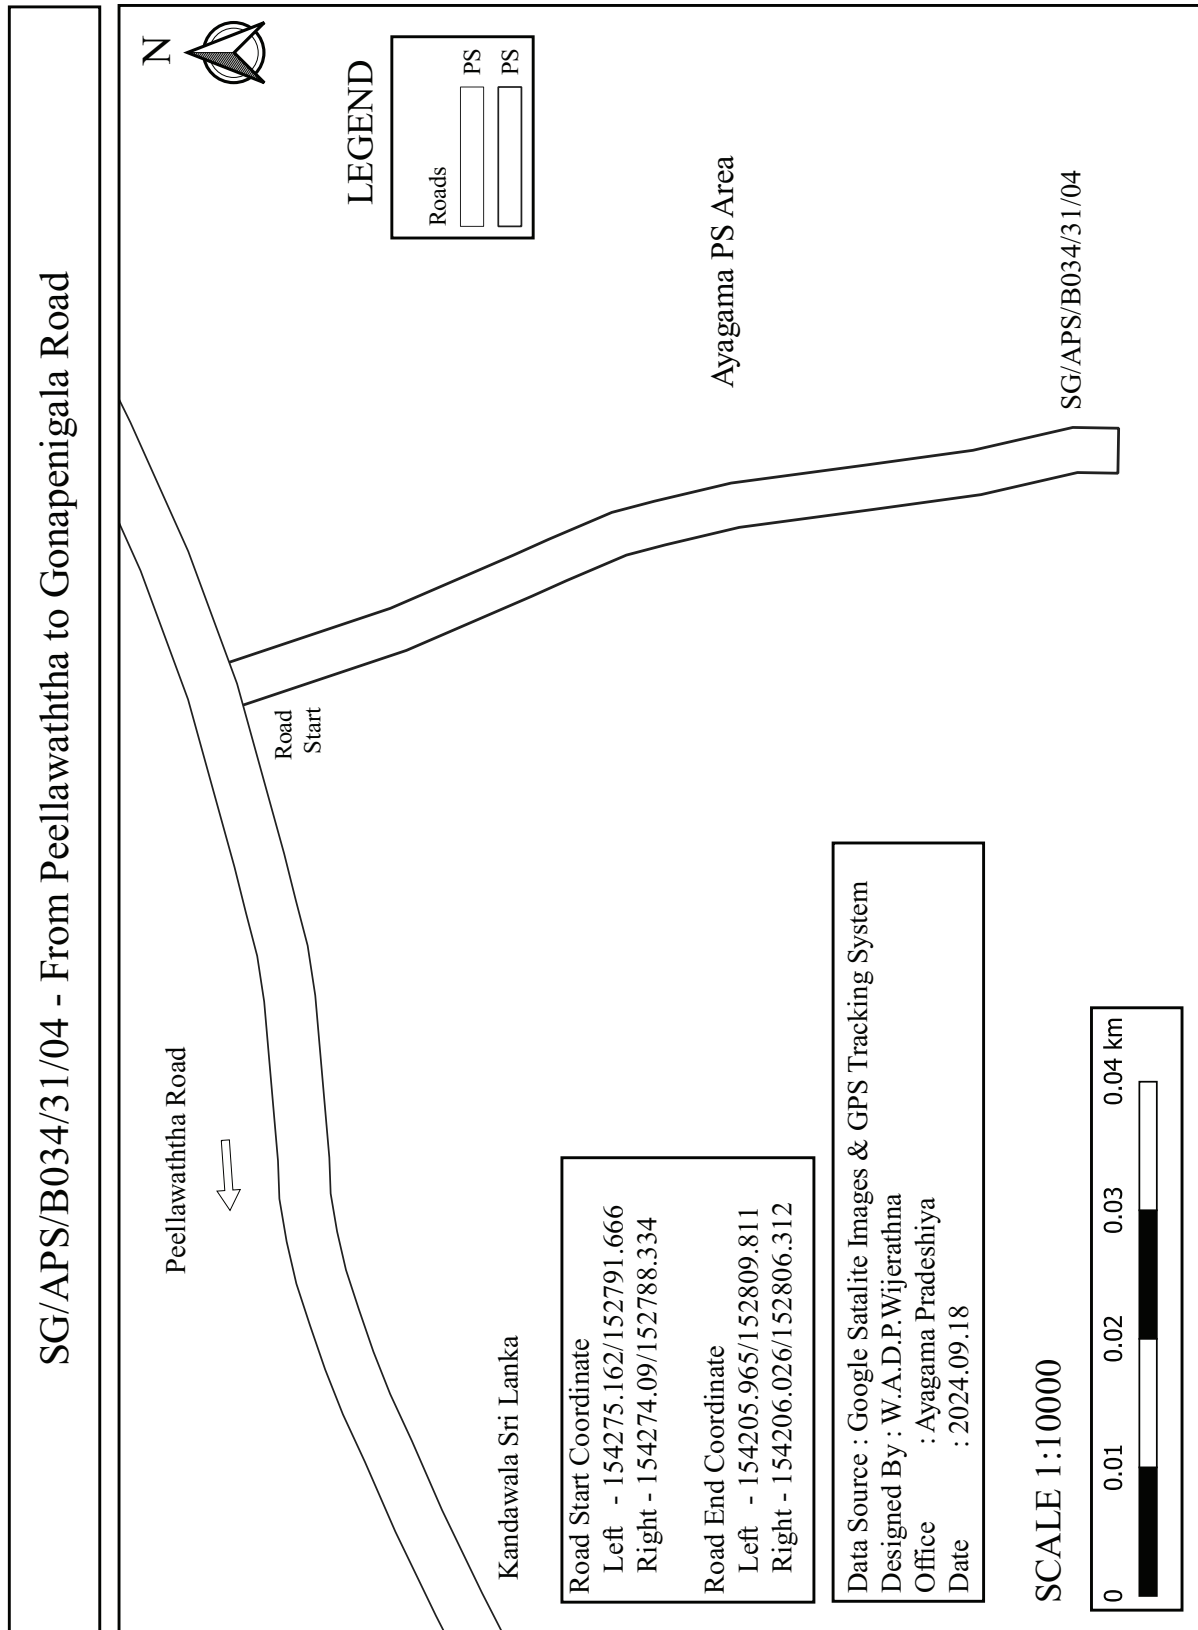


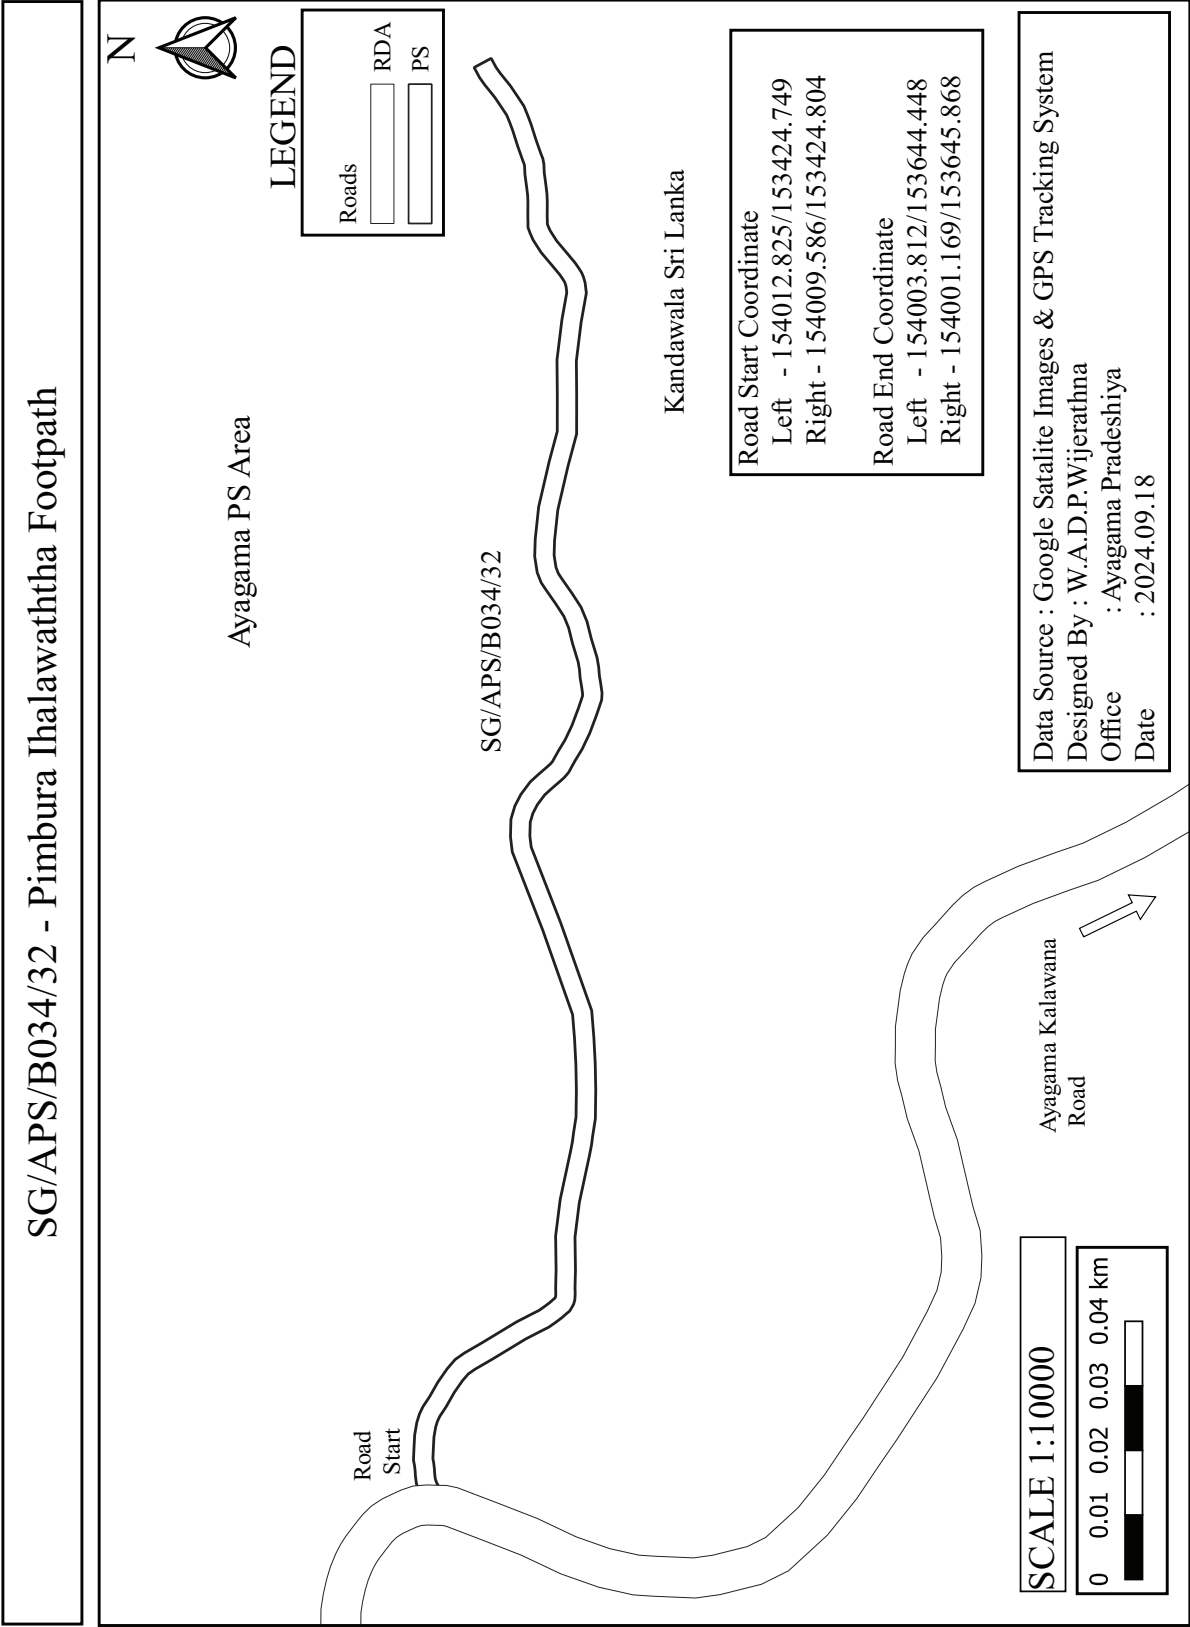


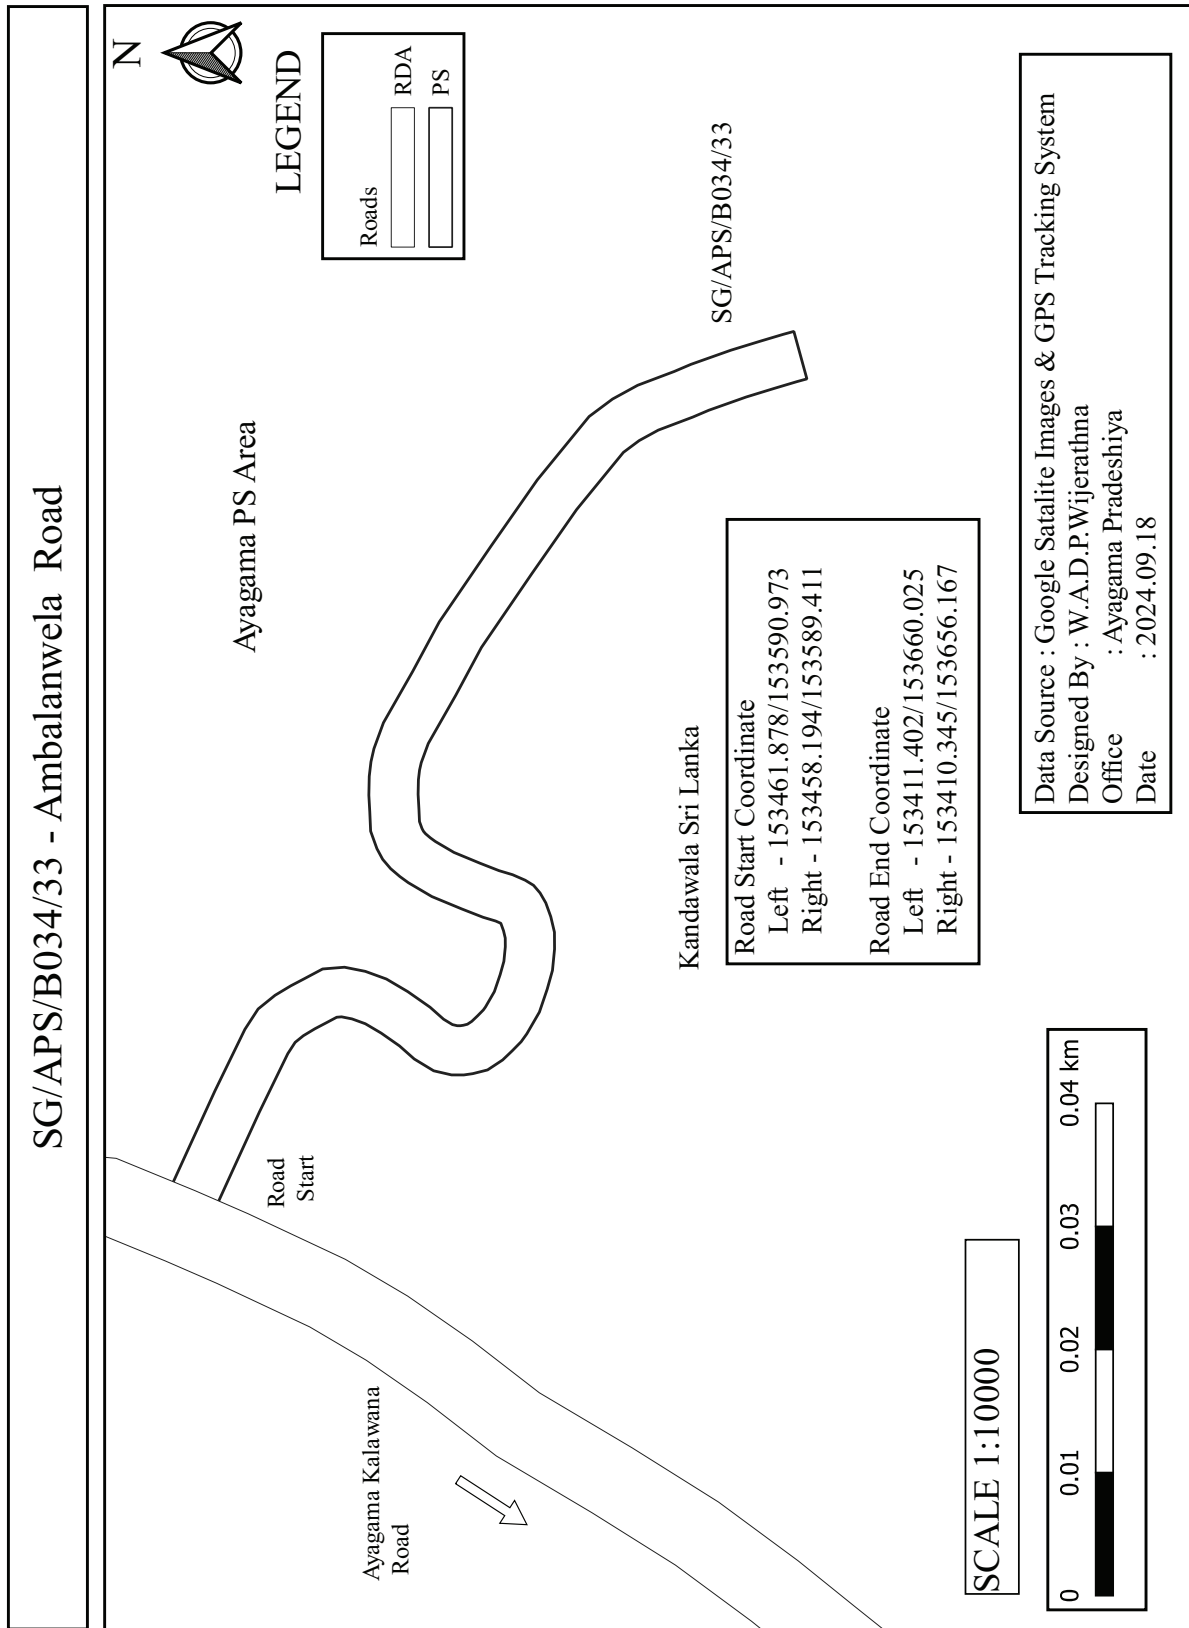


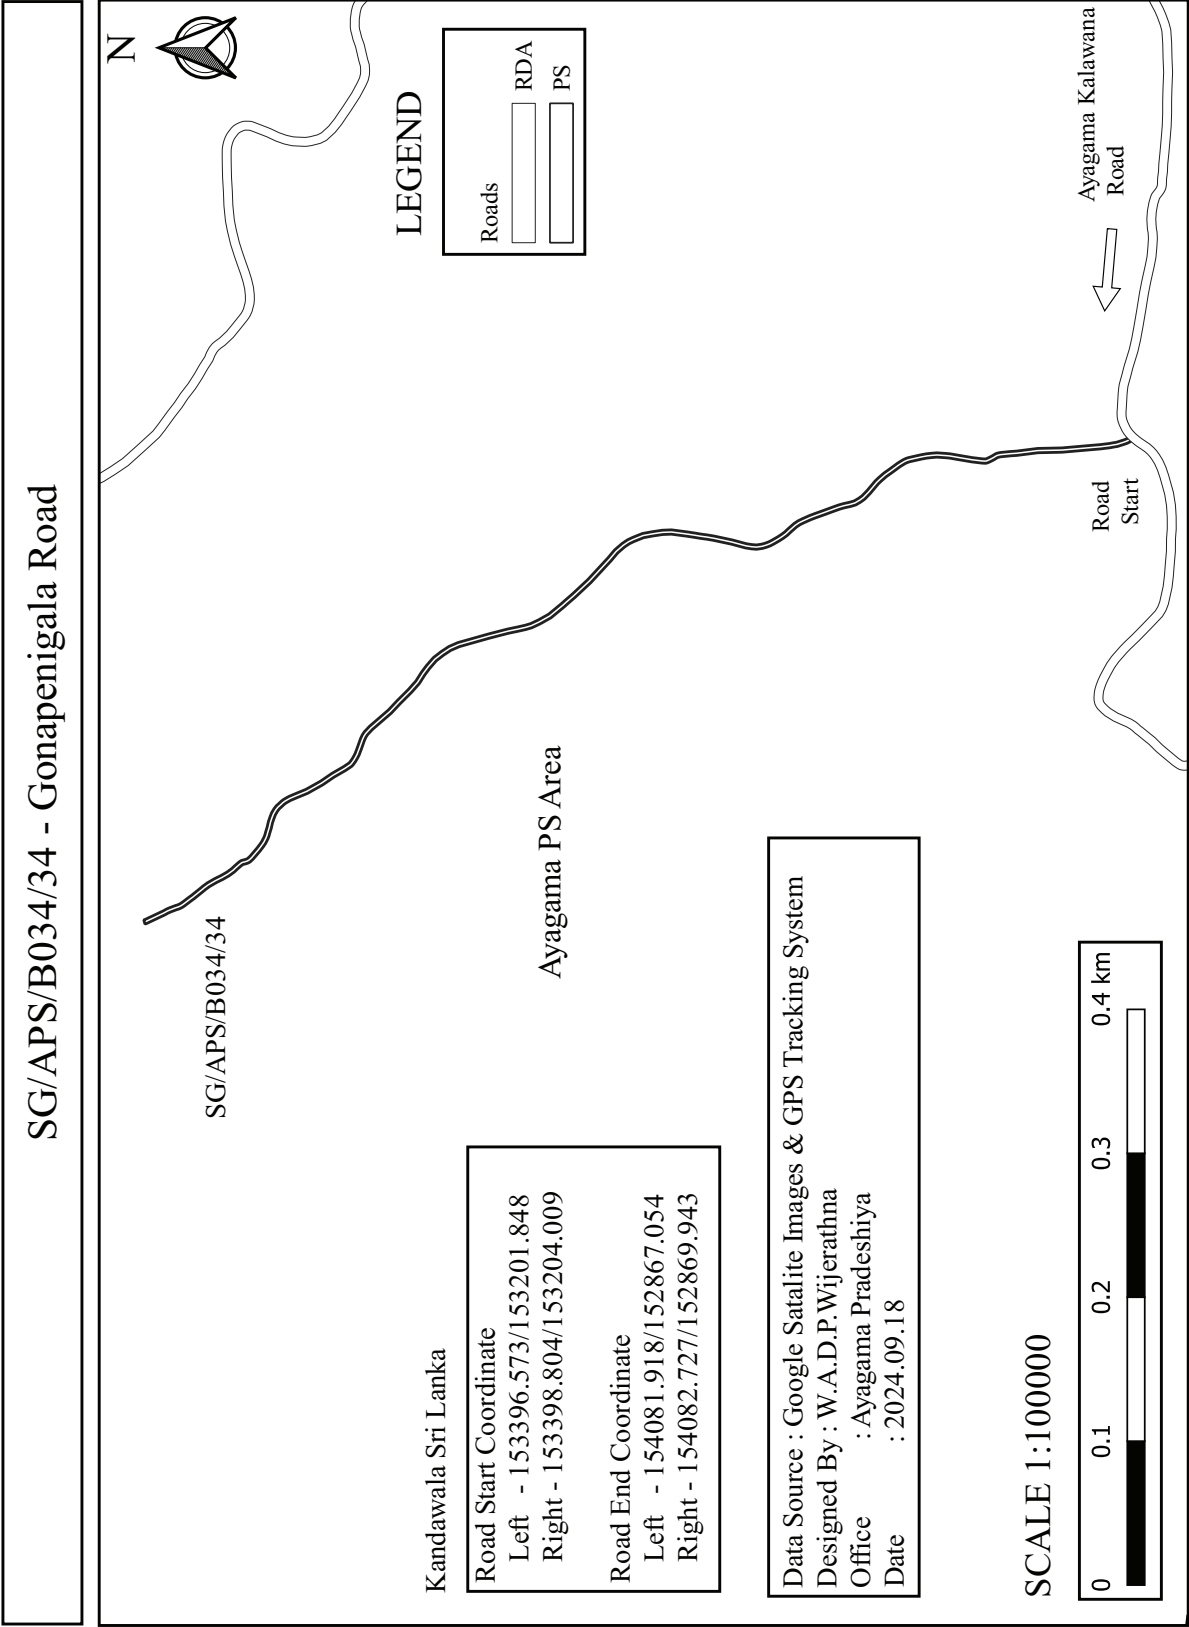




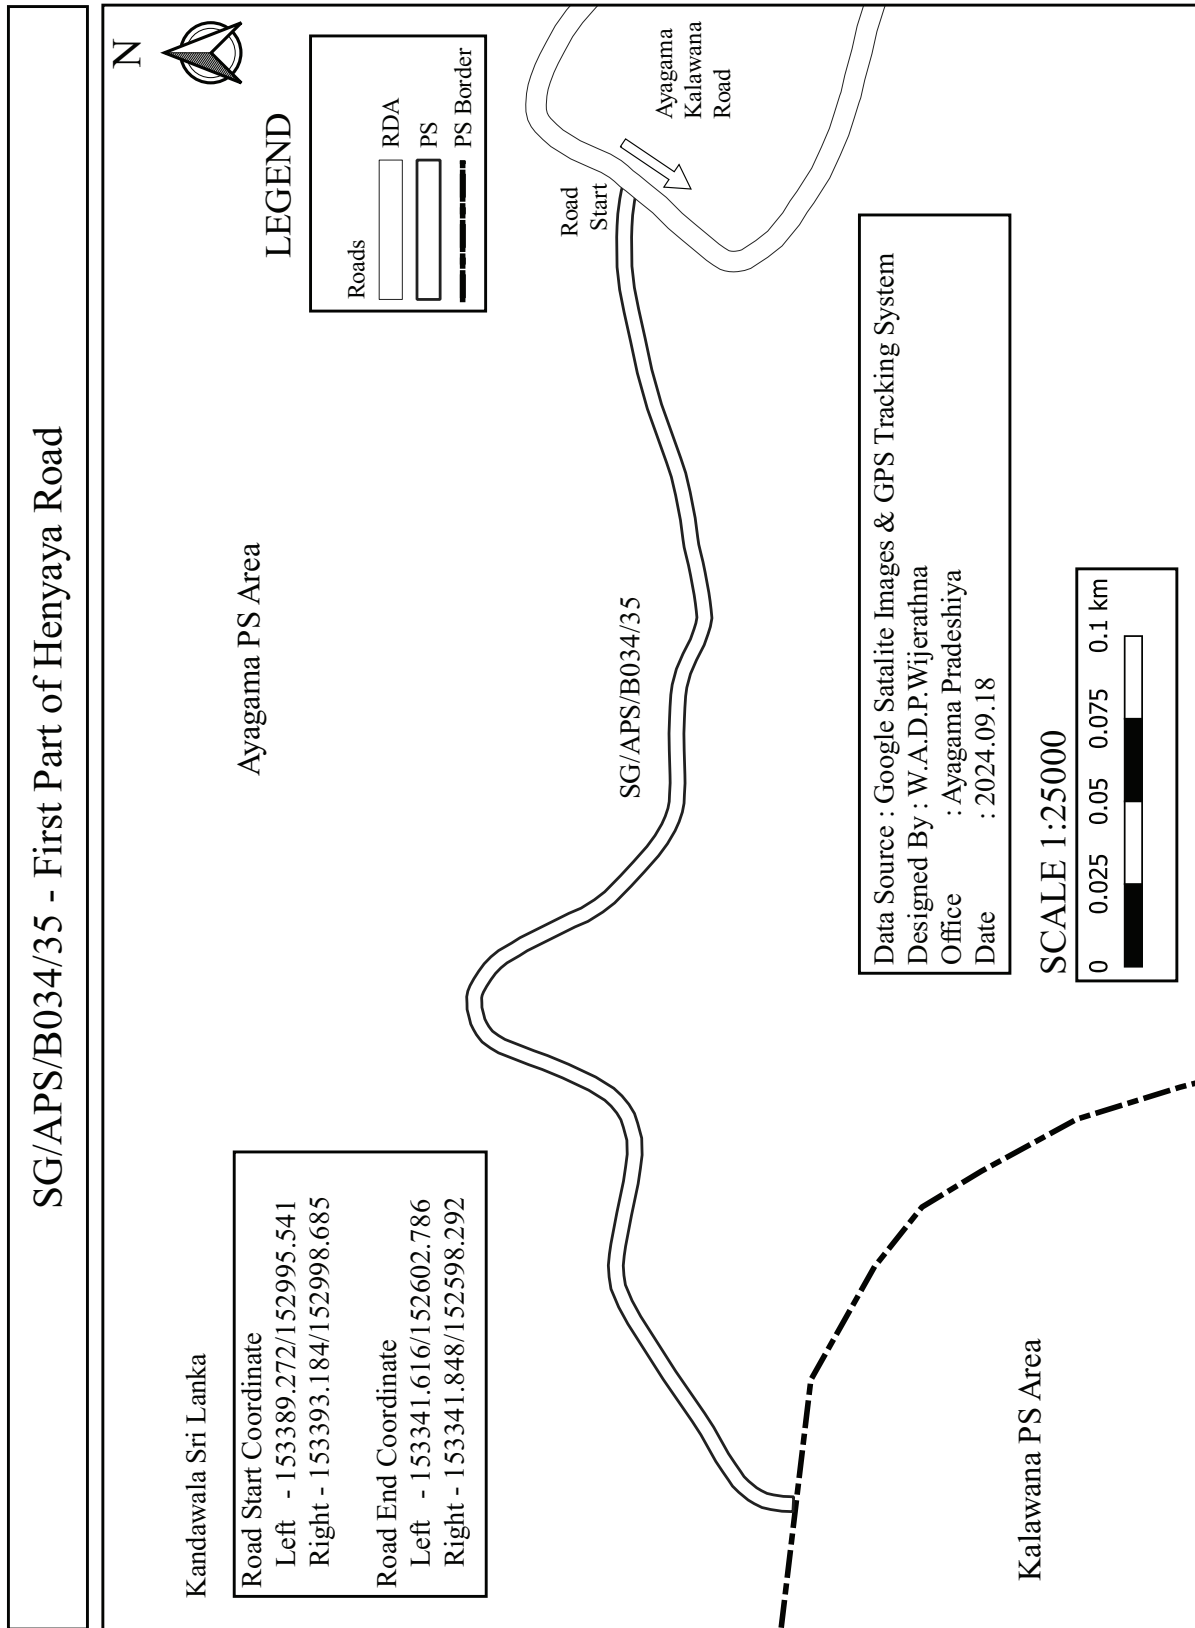


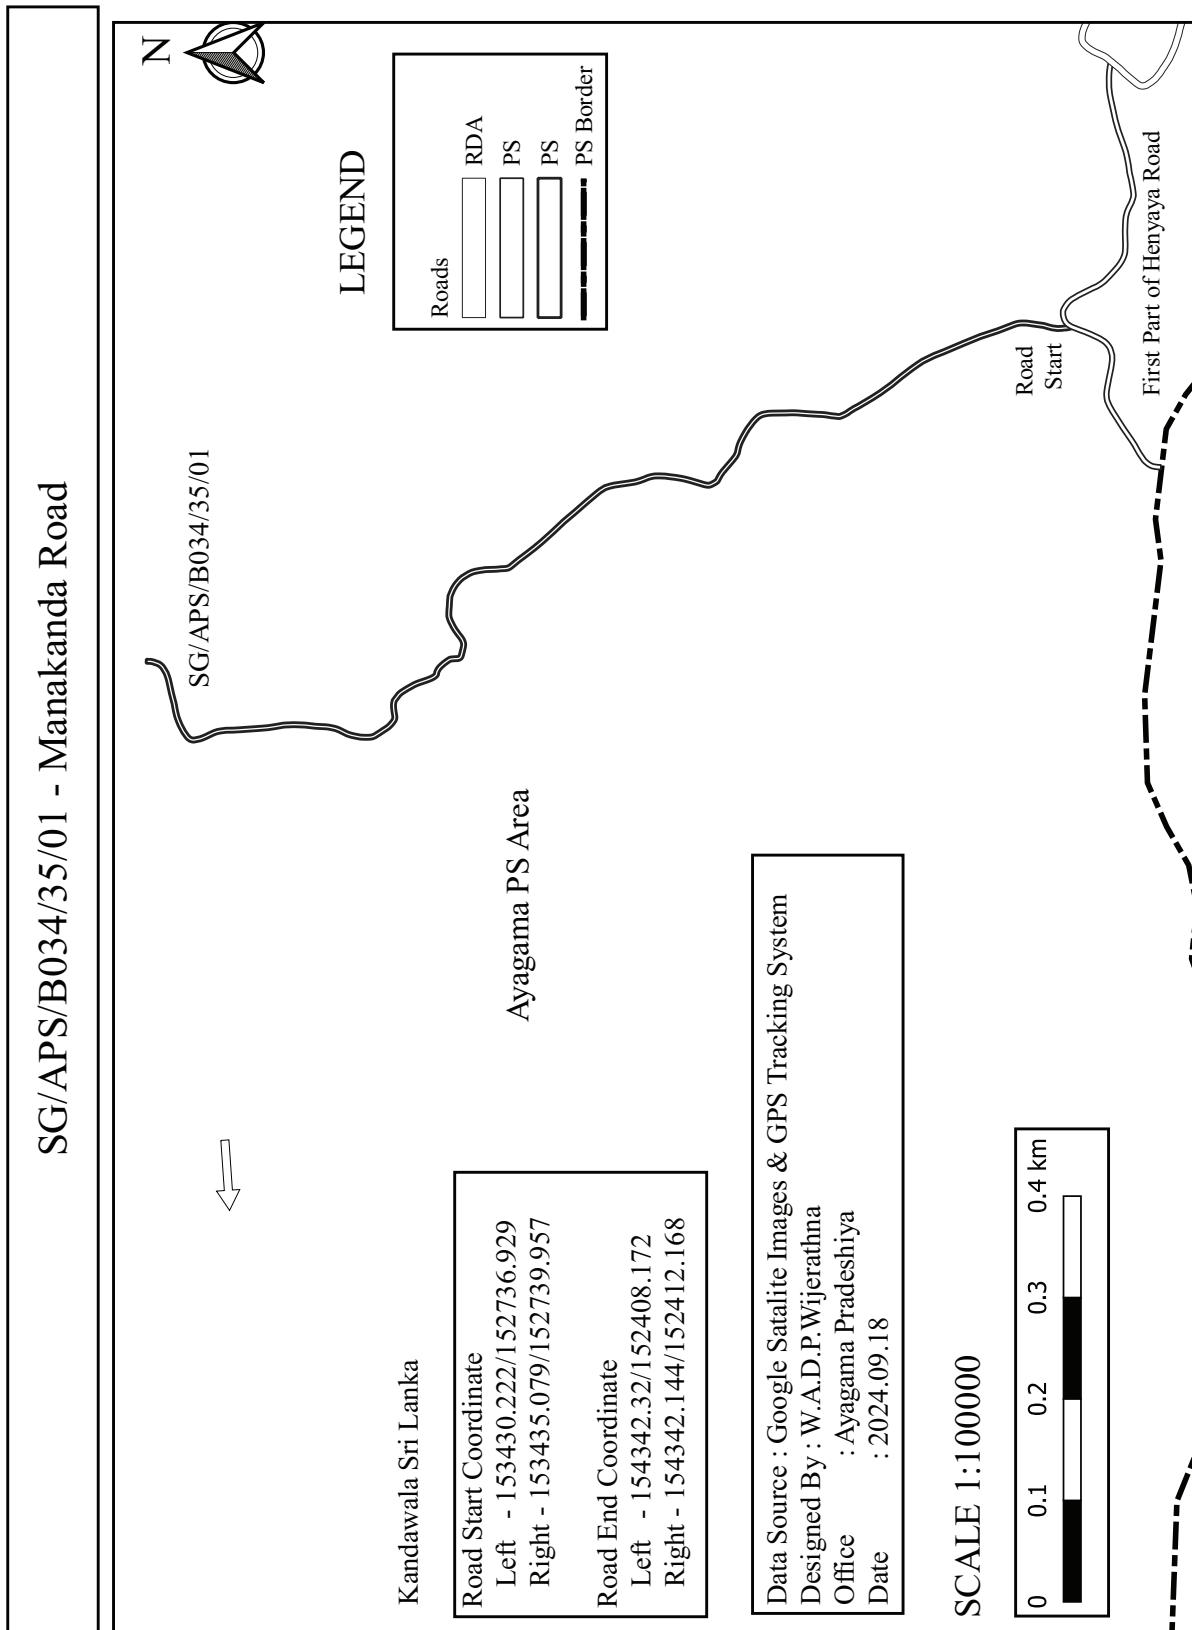


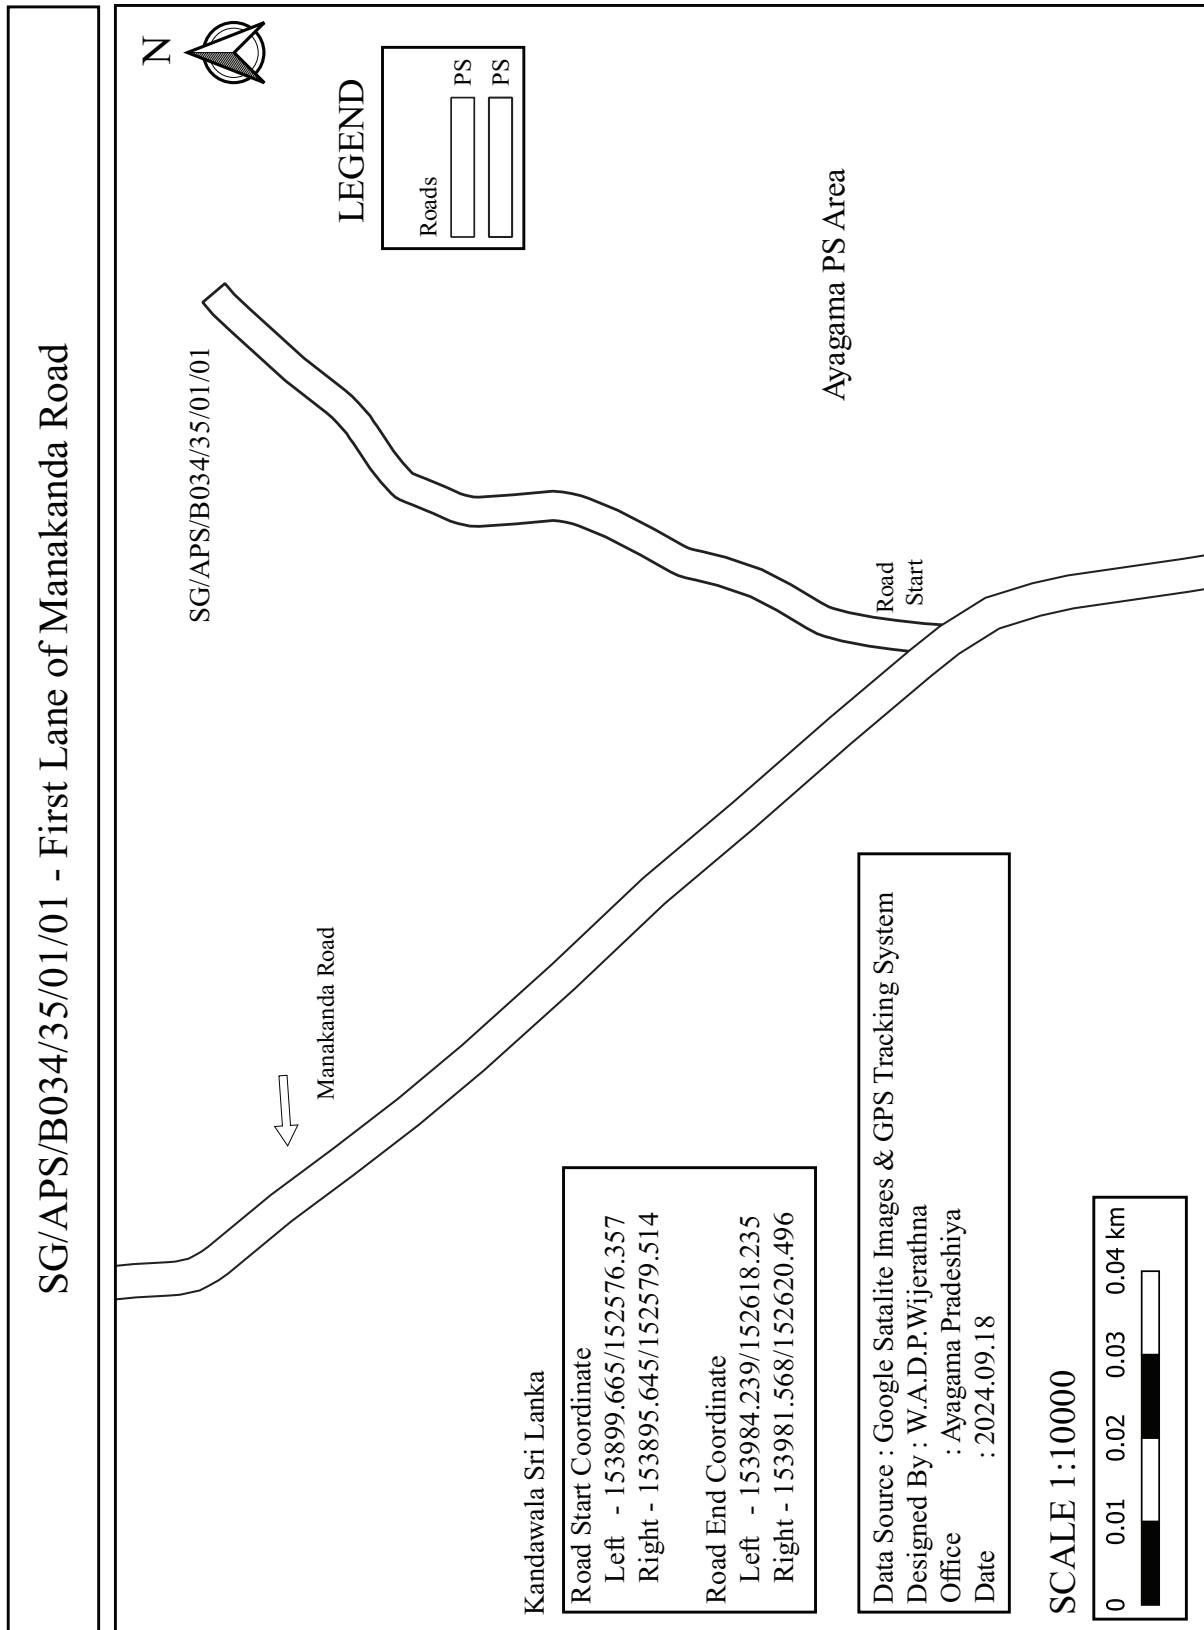


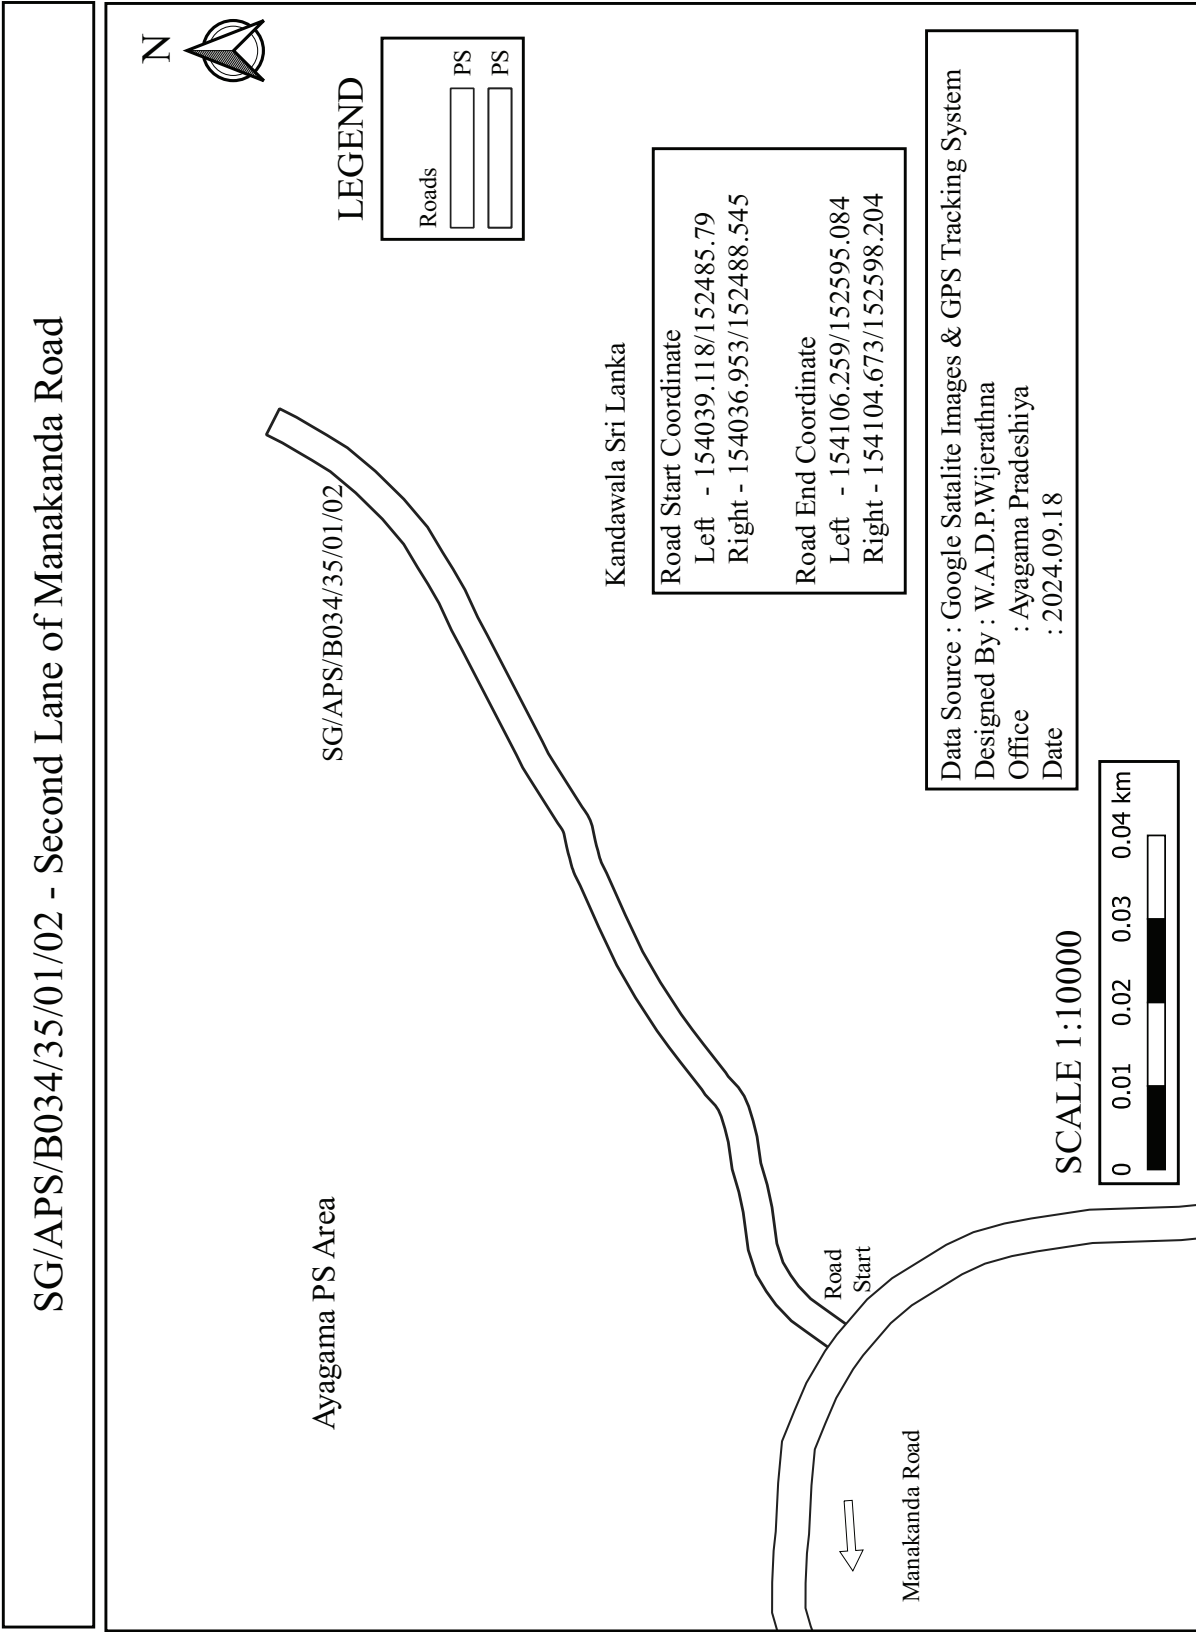


## SG/APS/B034/35/01/03 - Third Lane of Manakanda Road

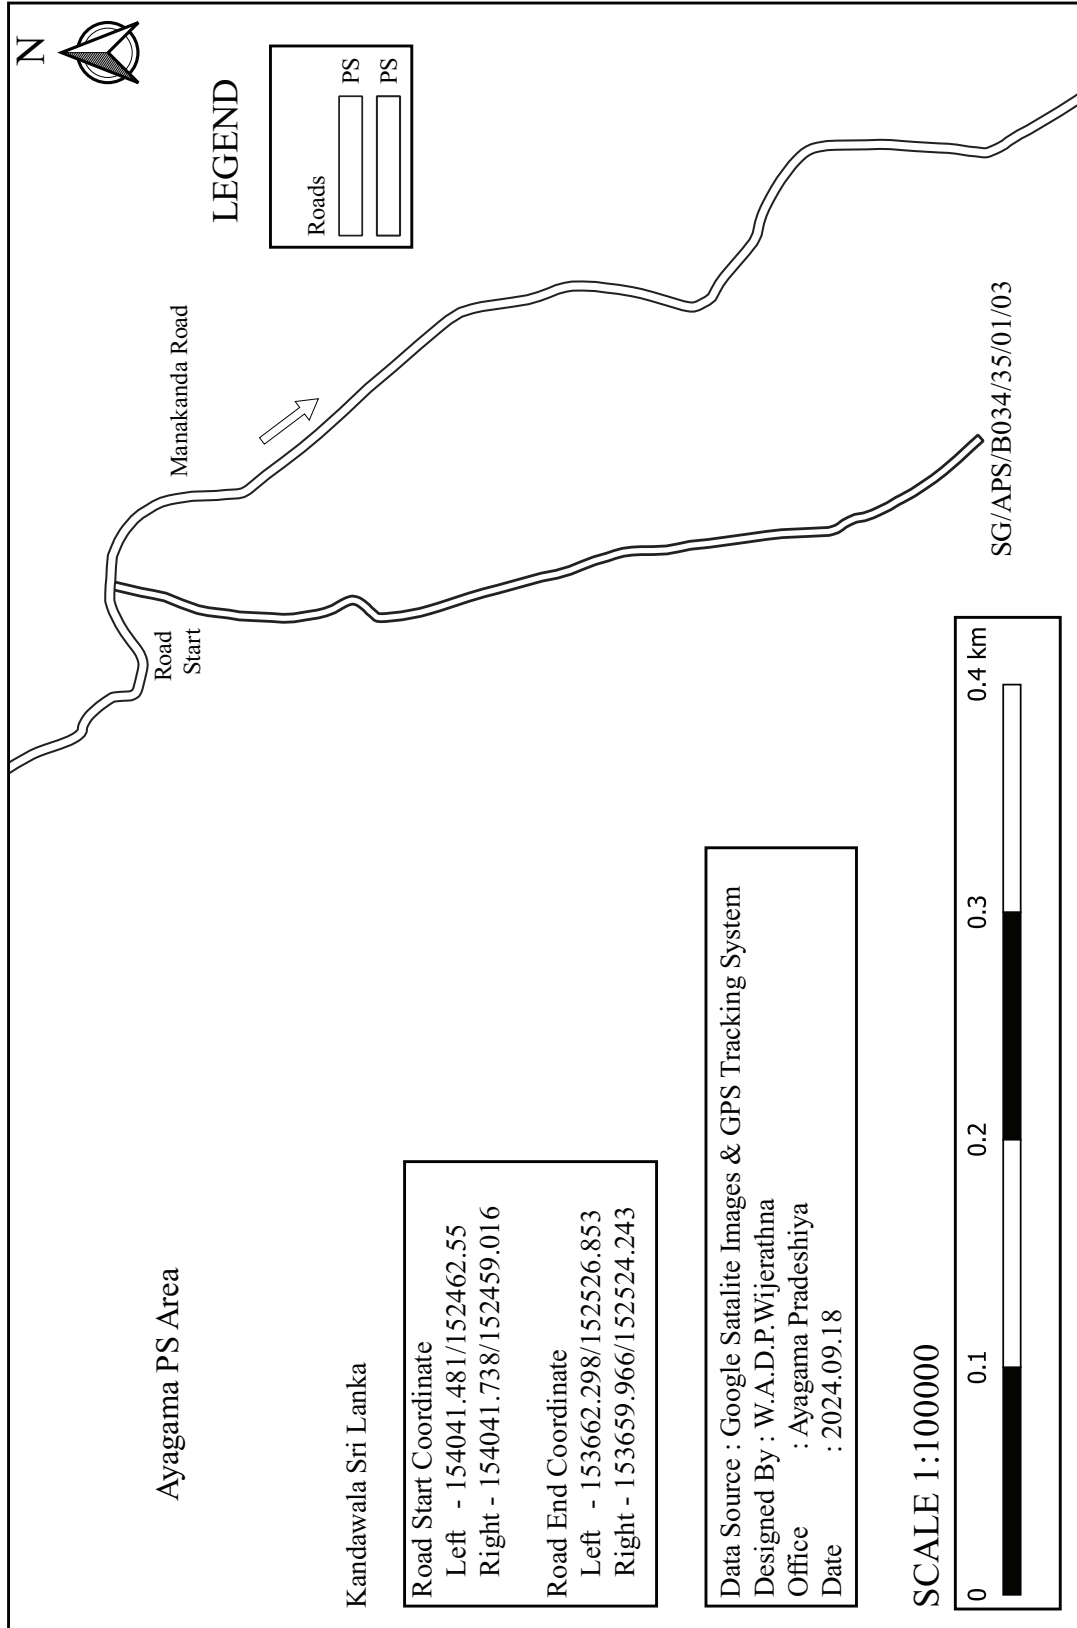


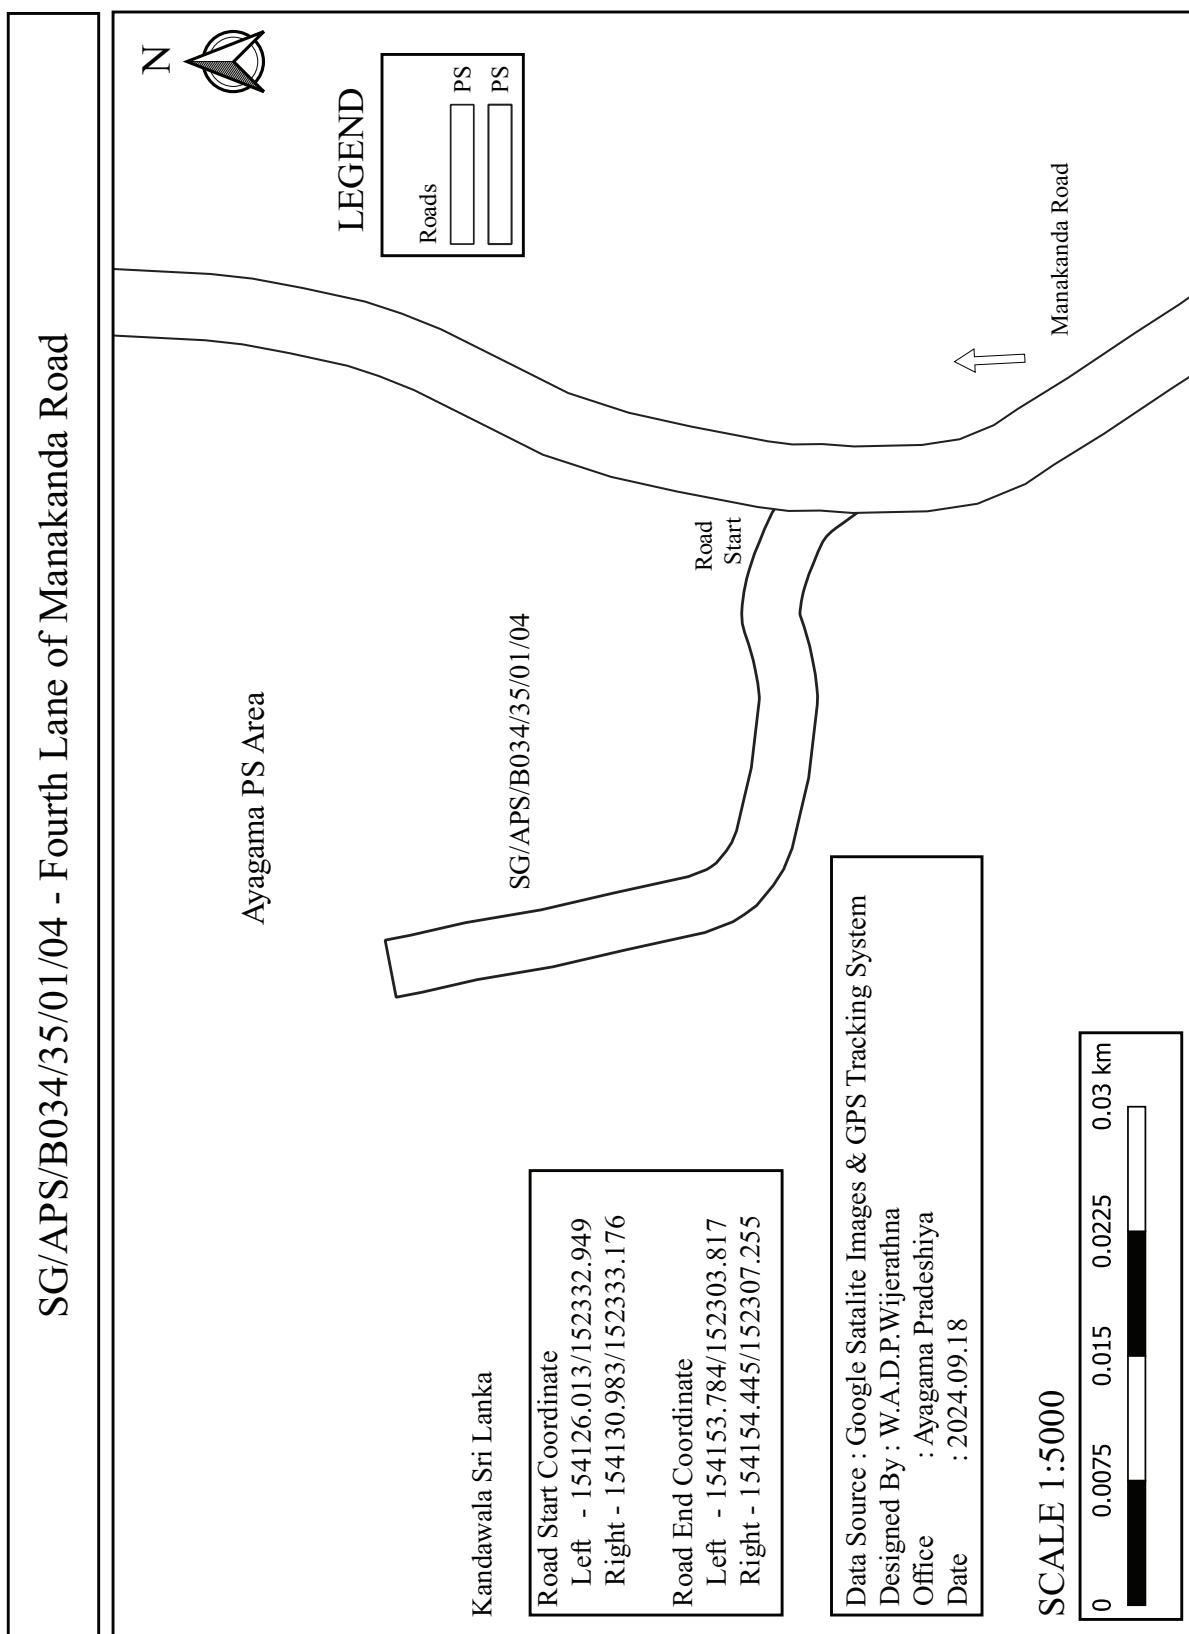


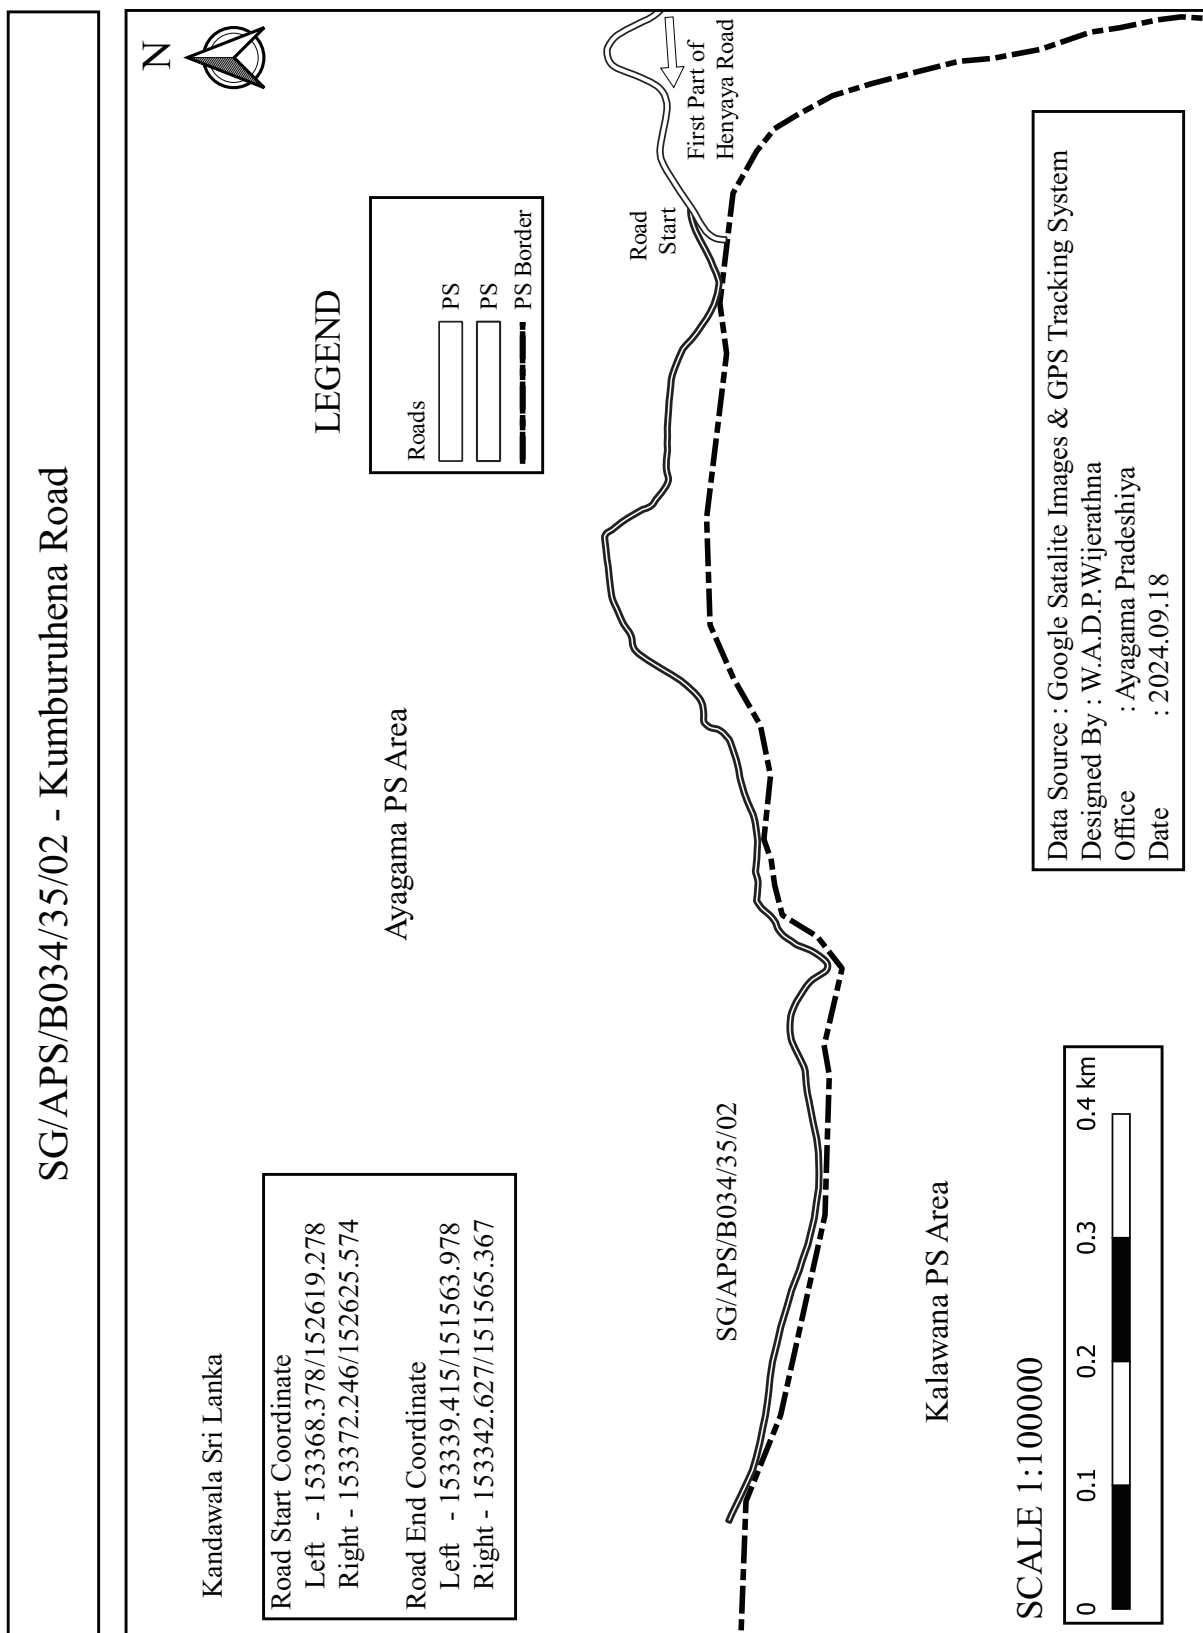


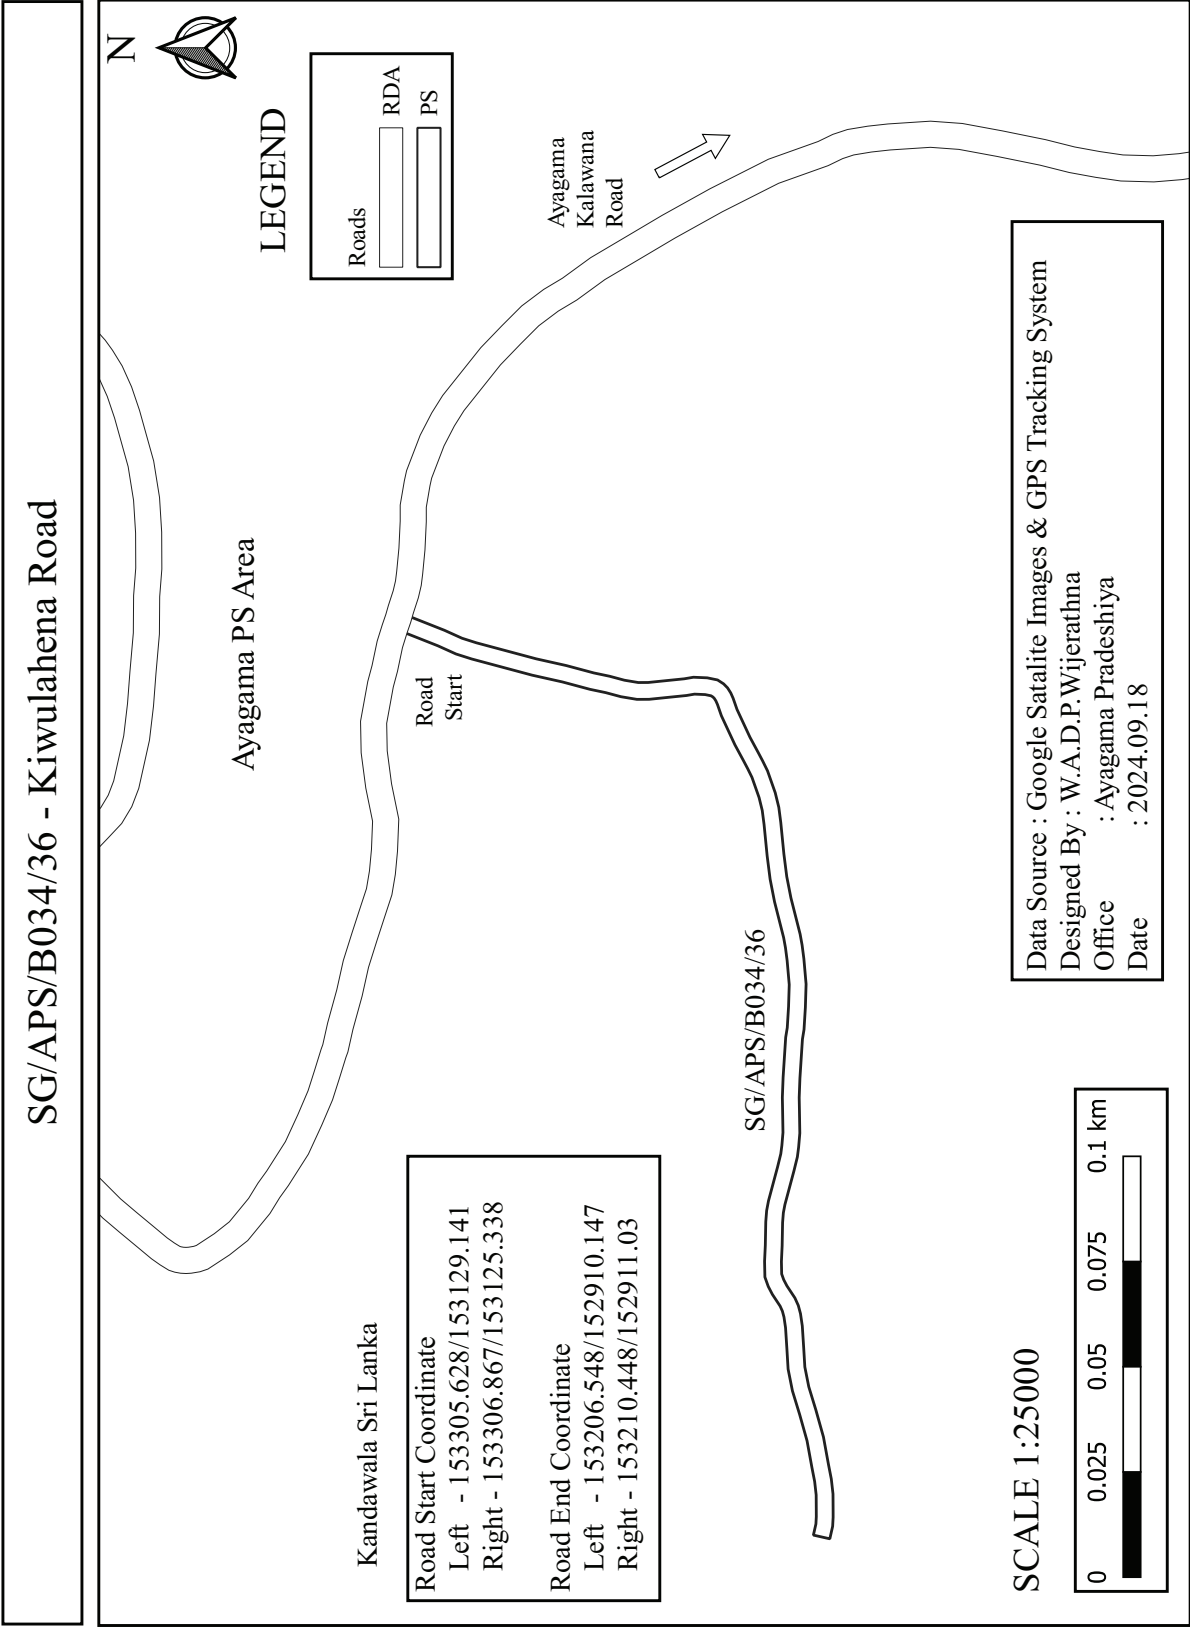





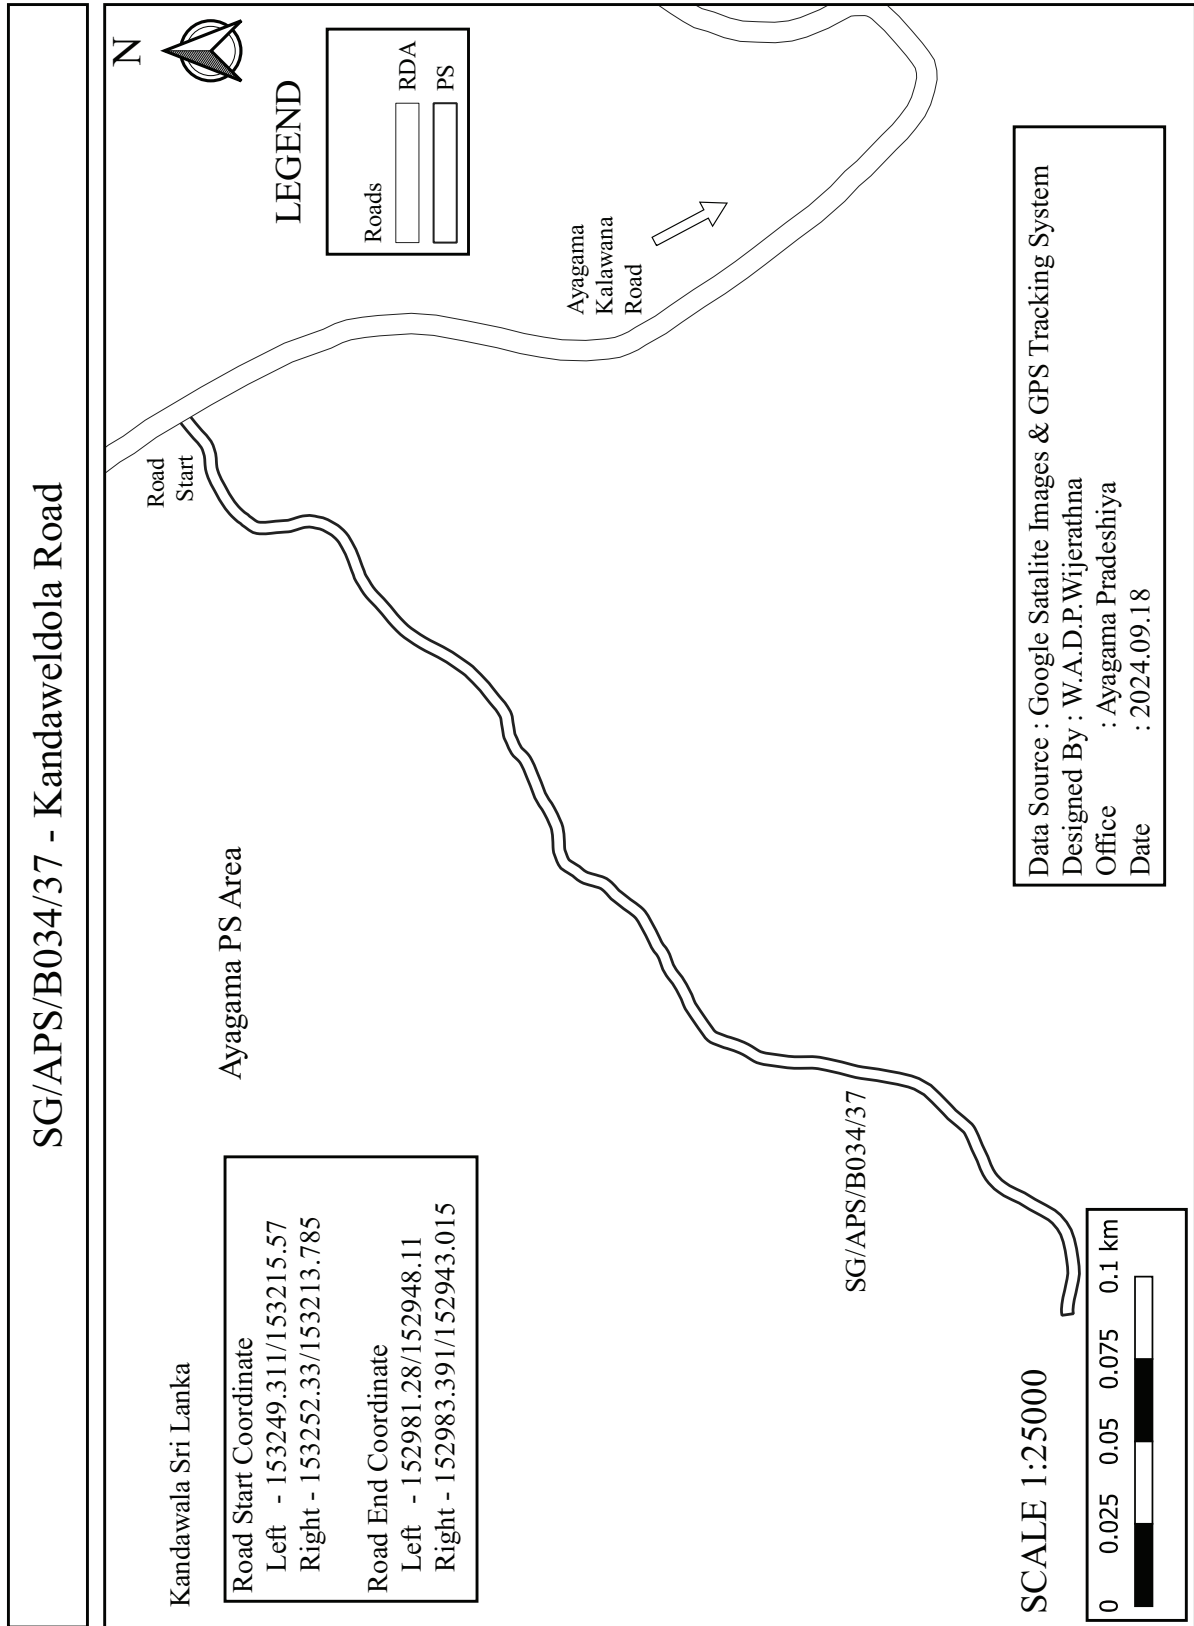


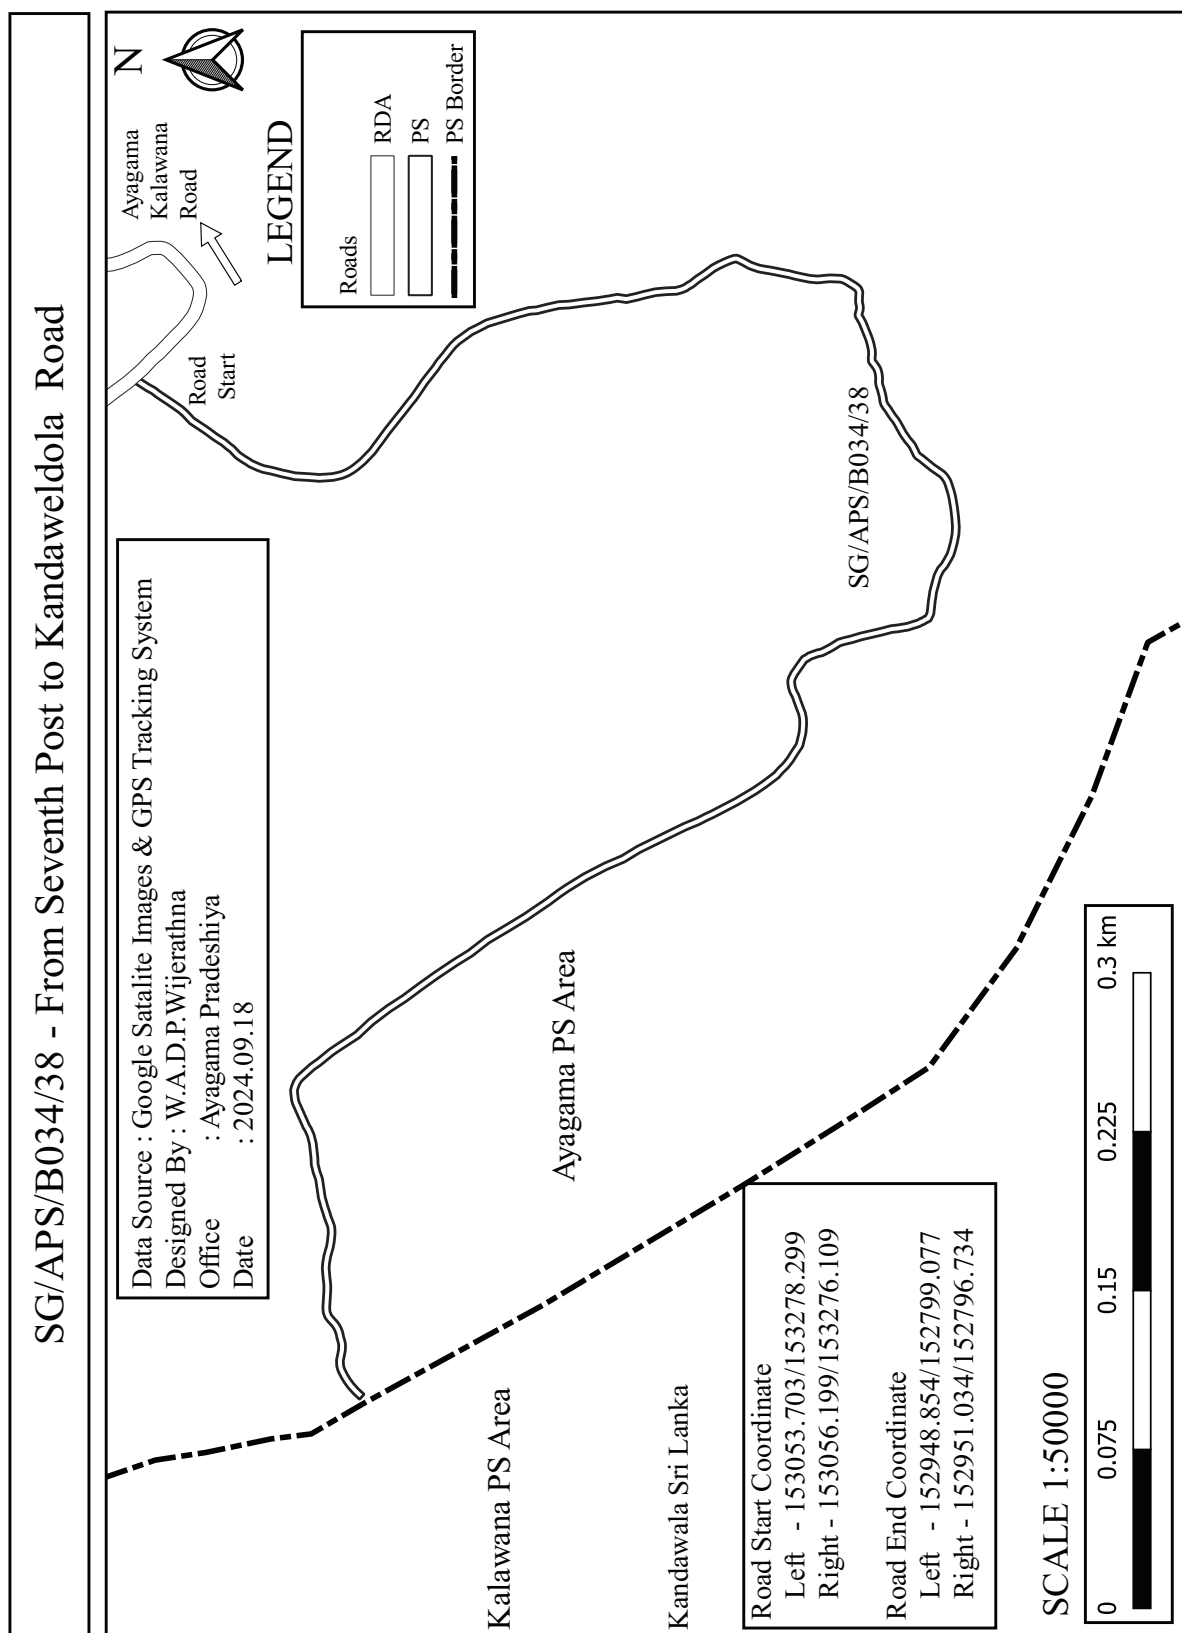


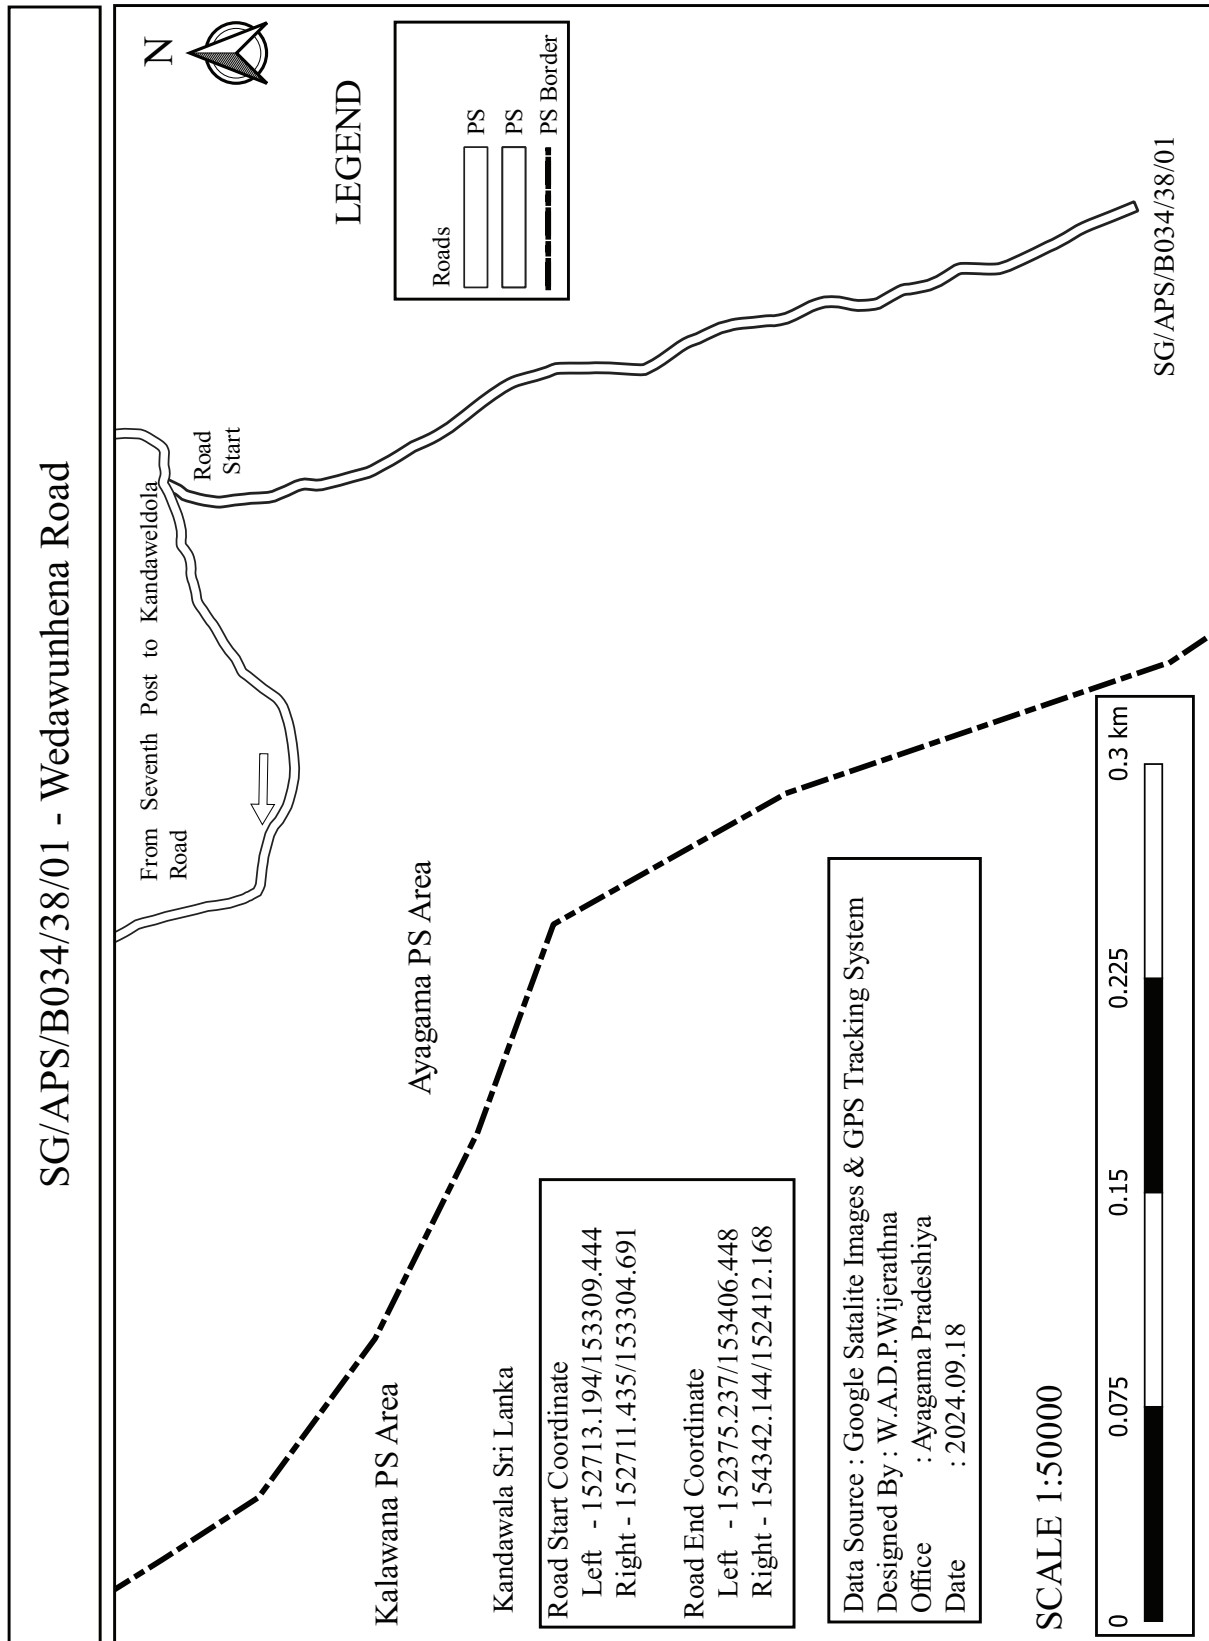


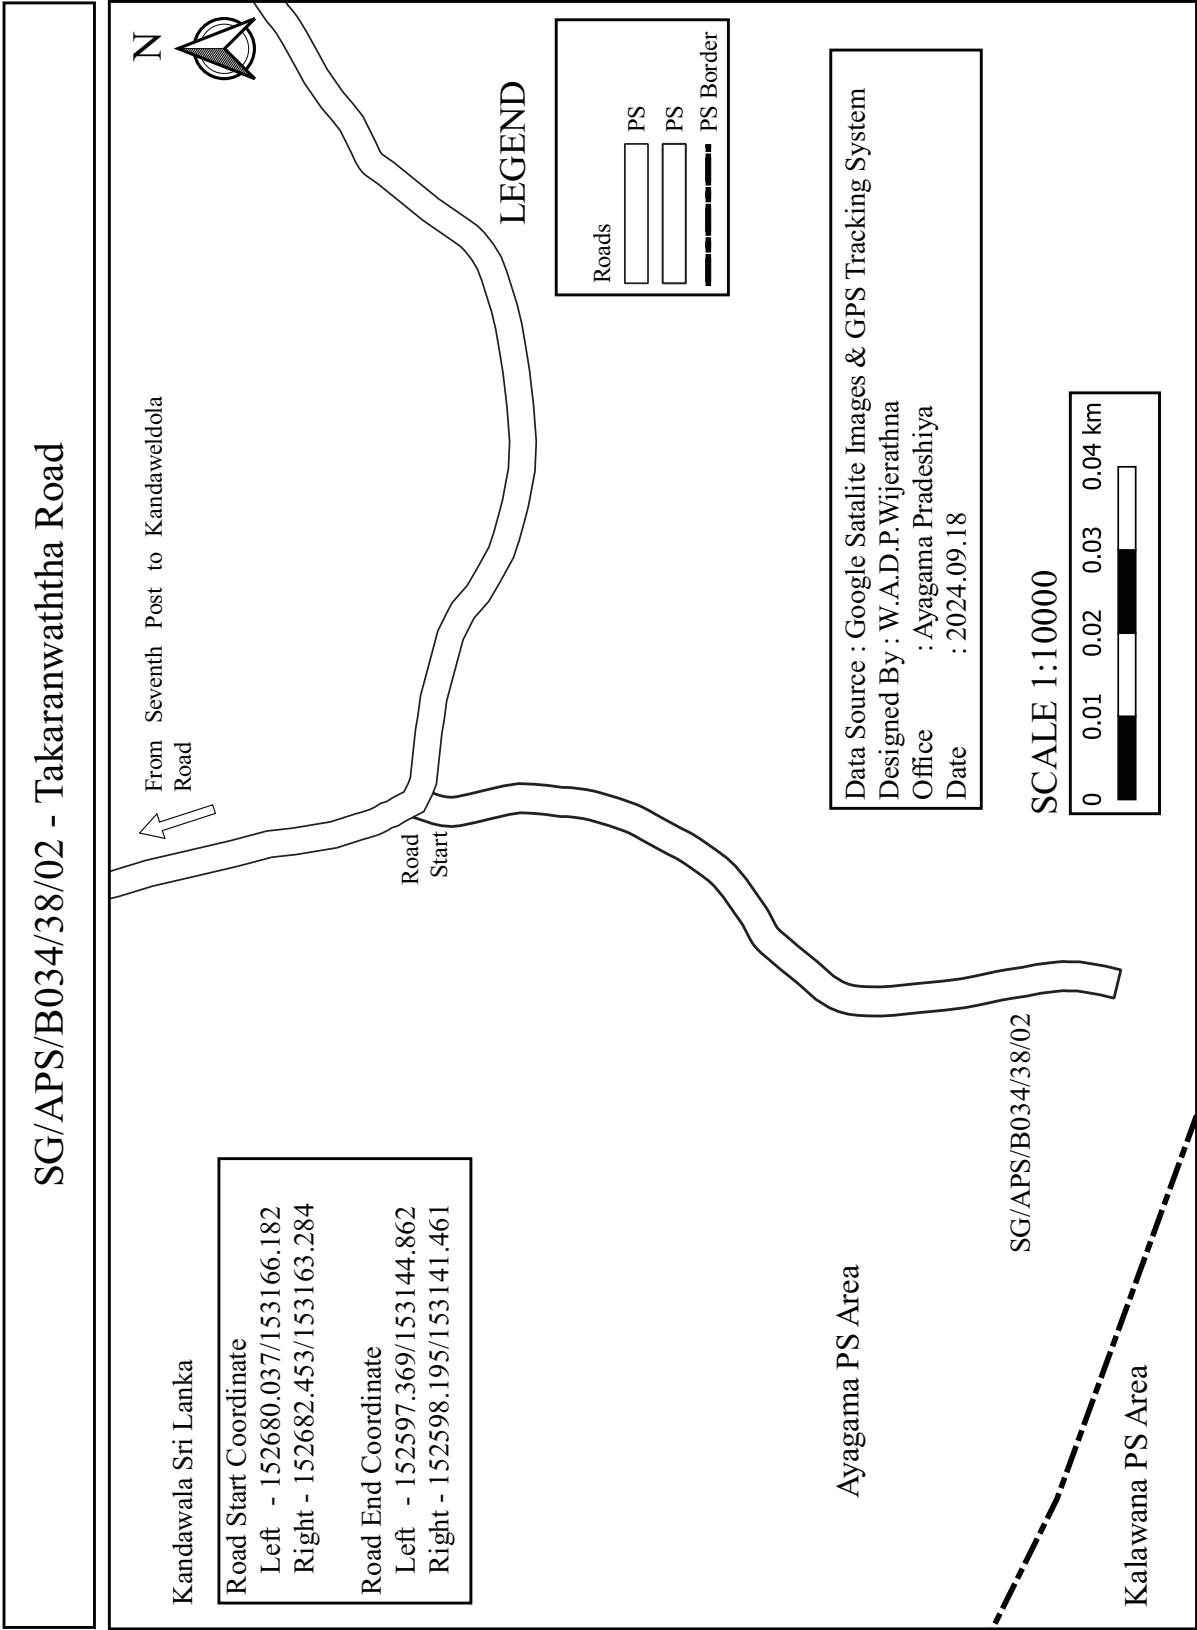

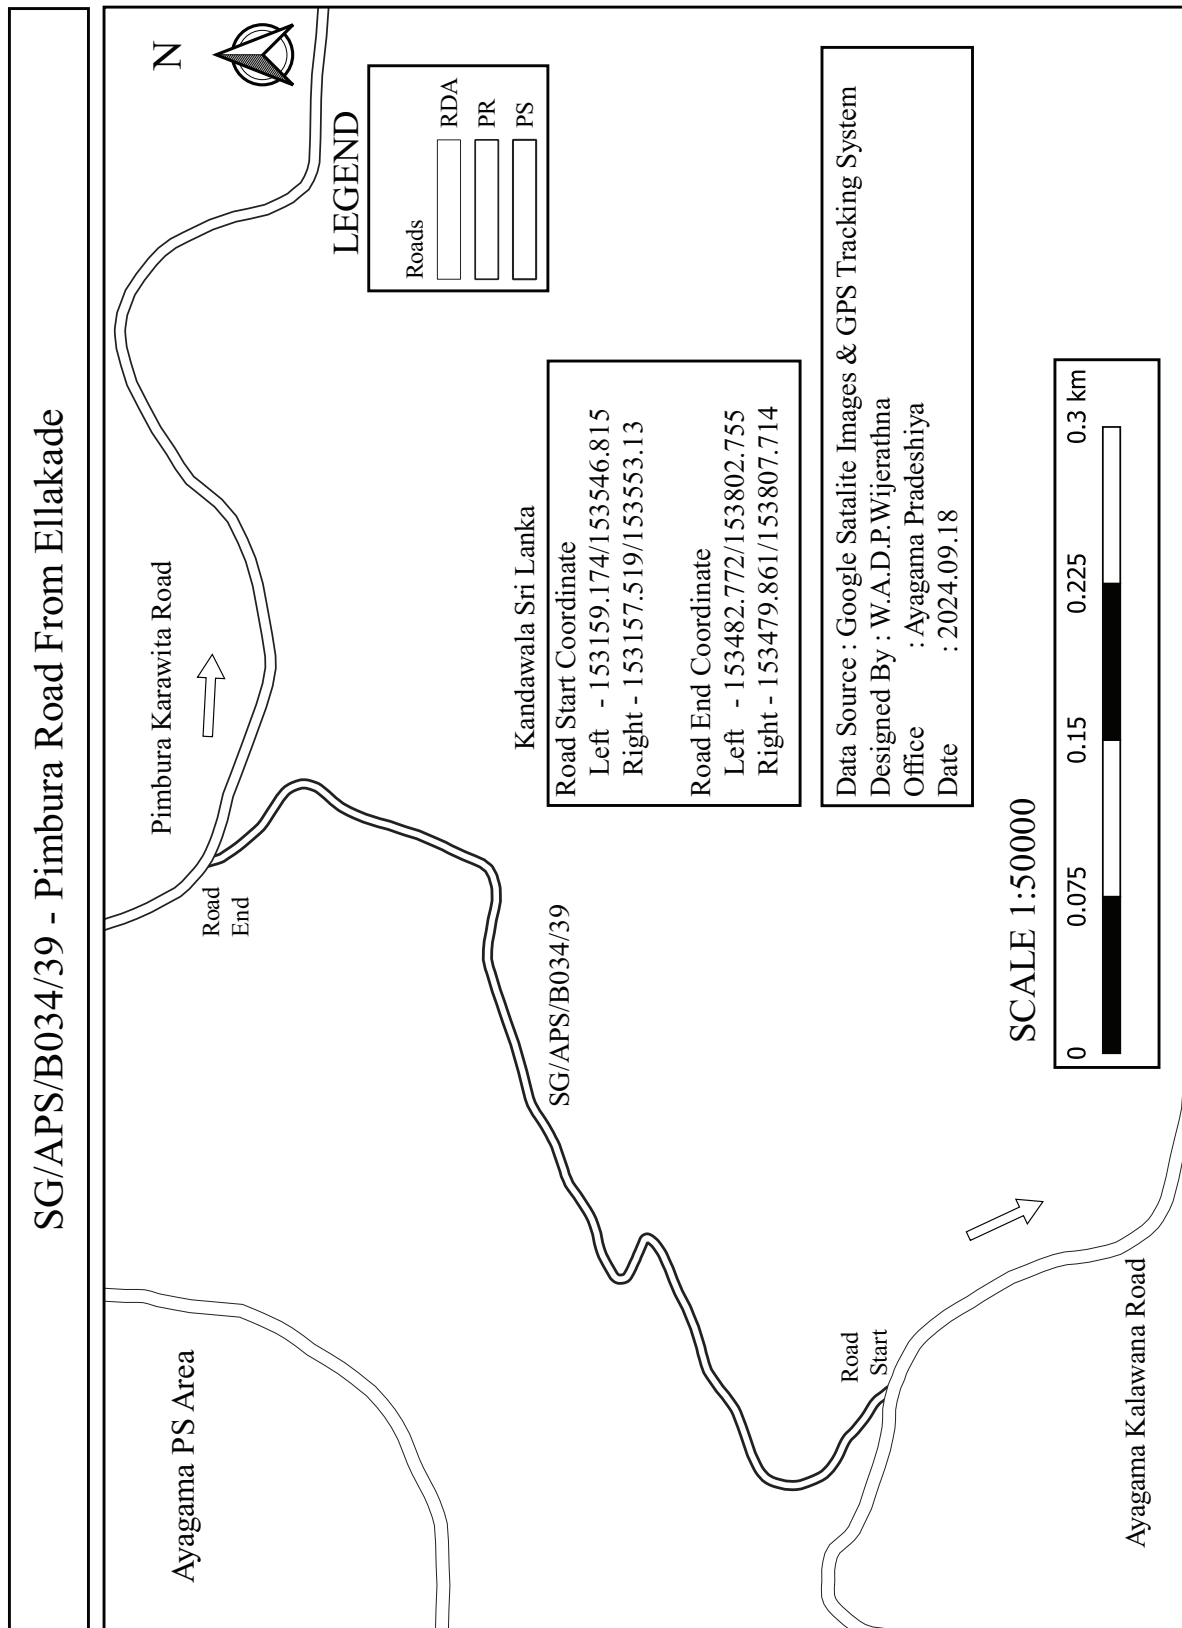


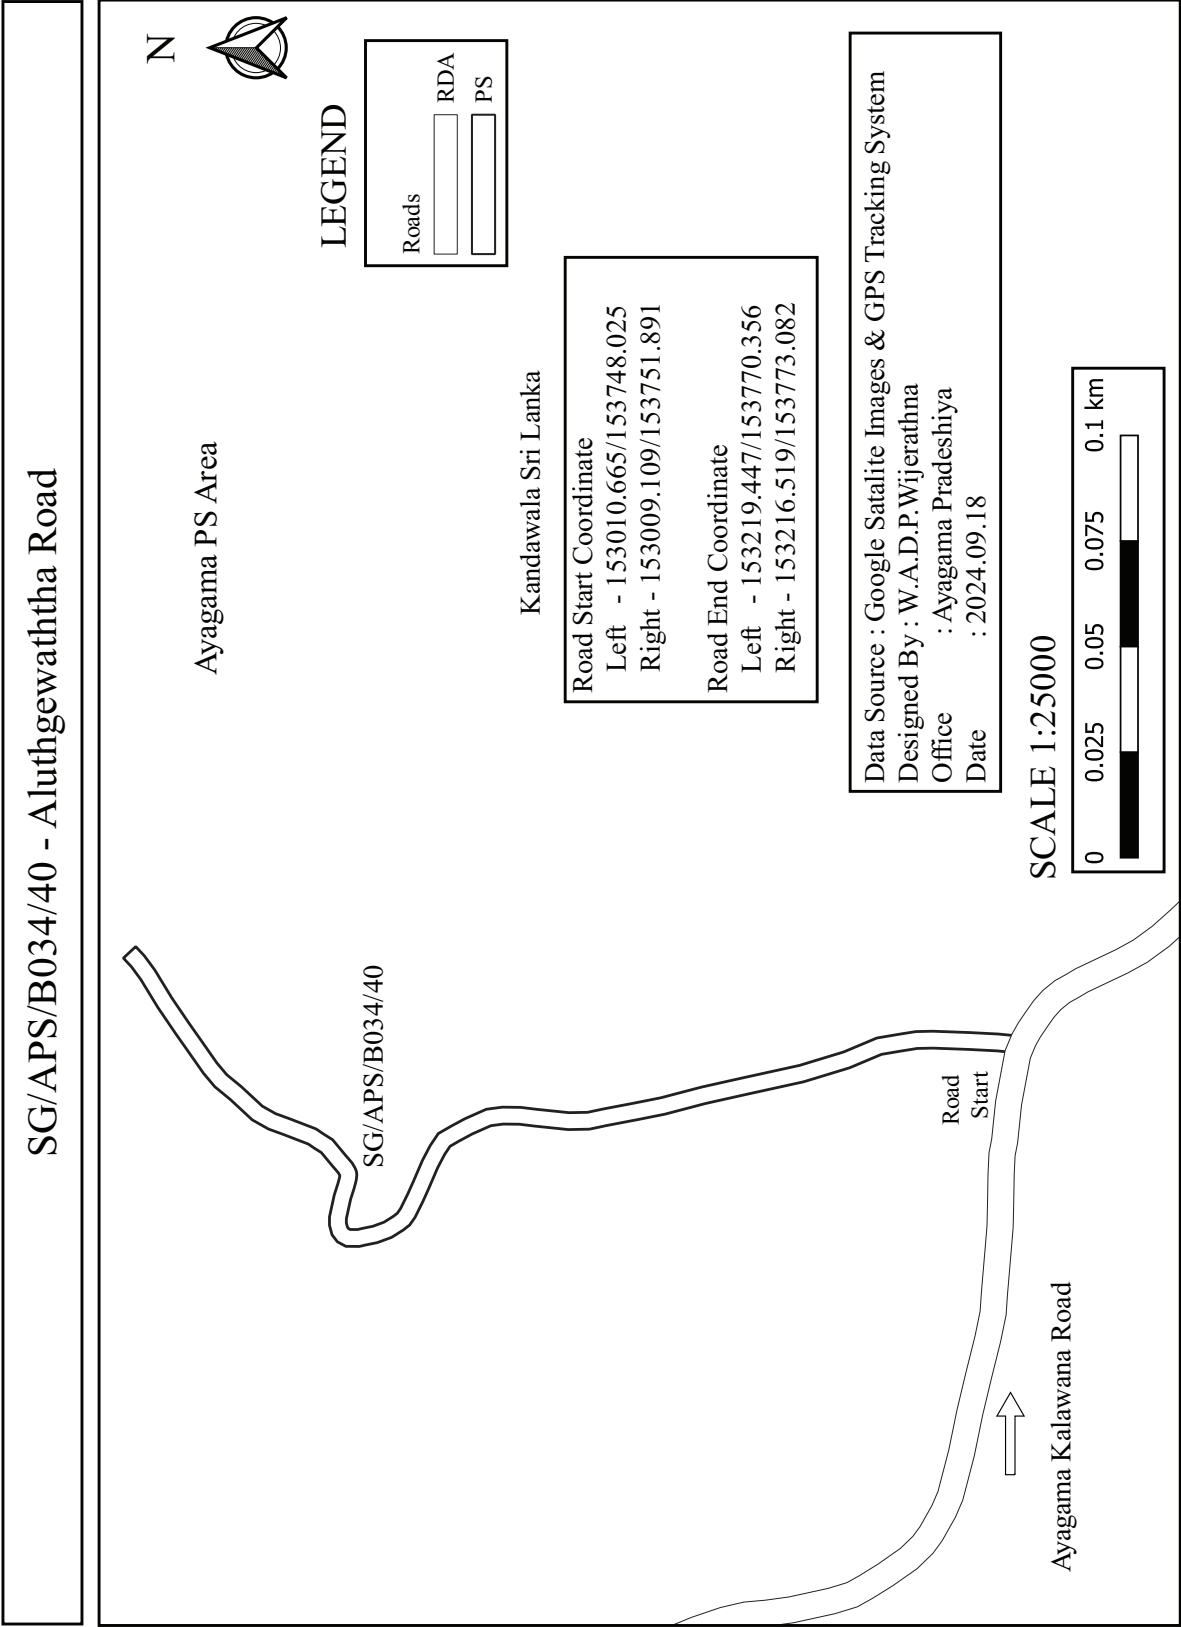


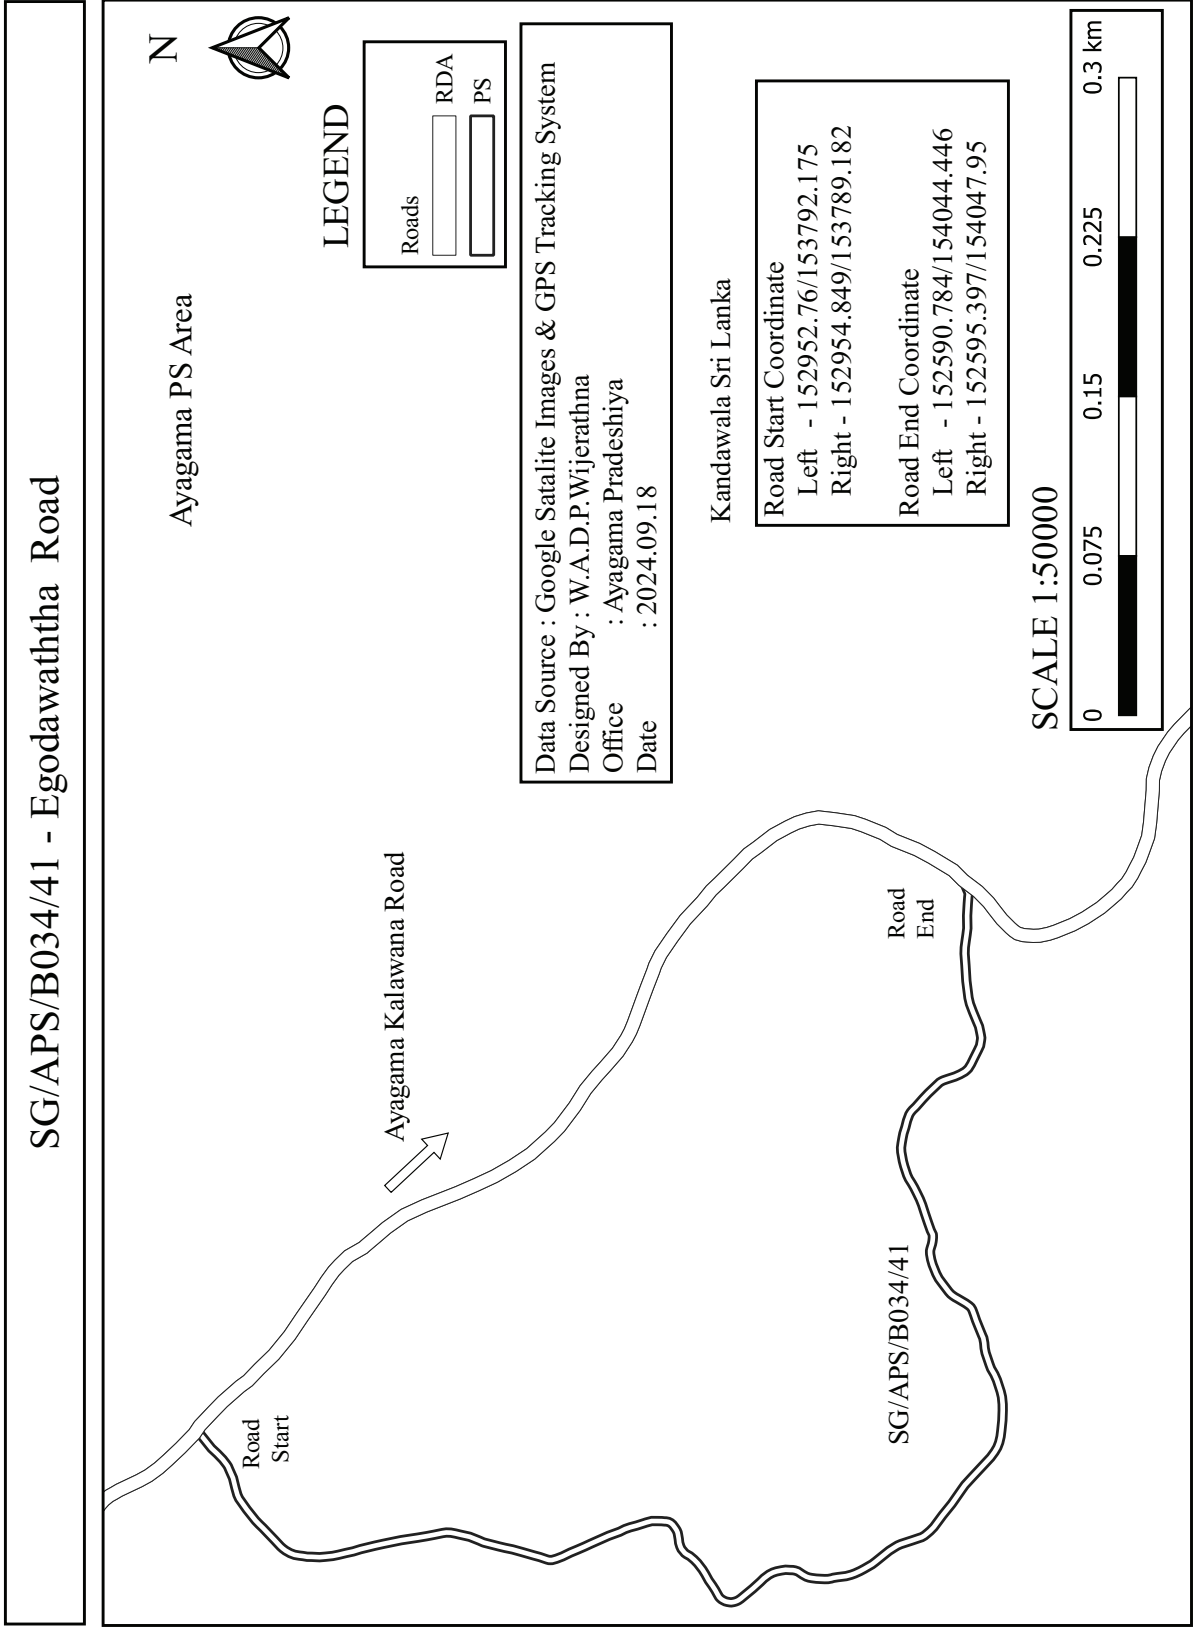


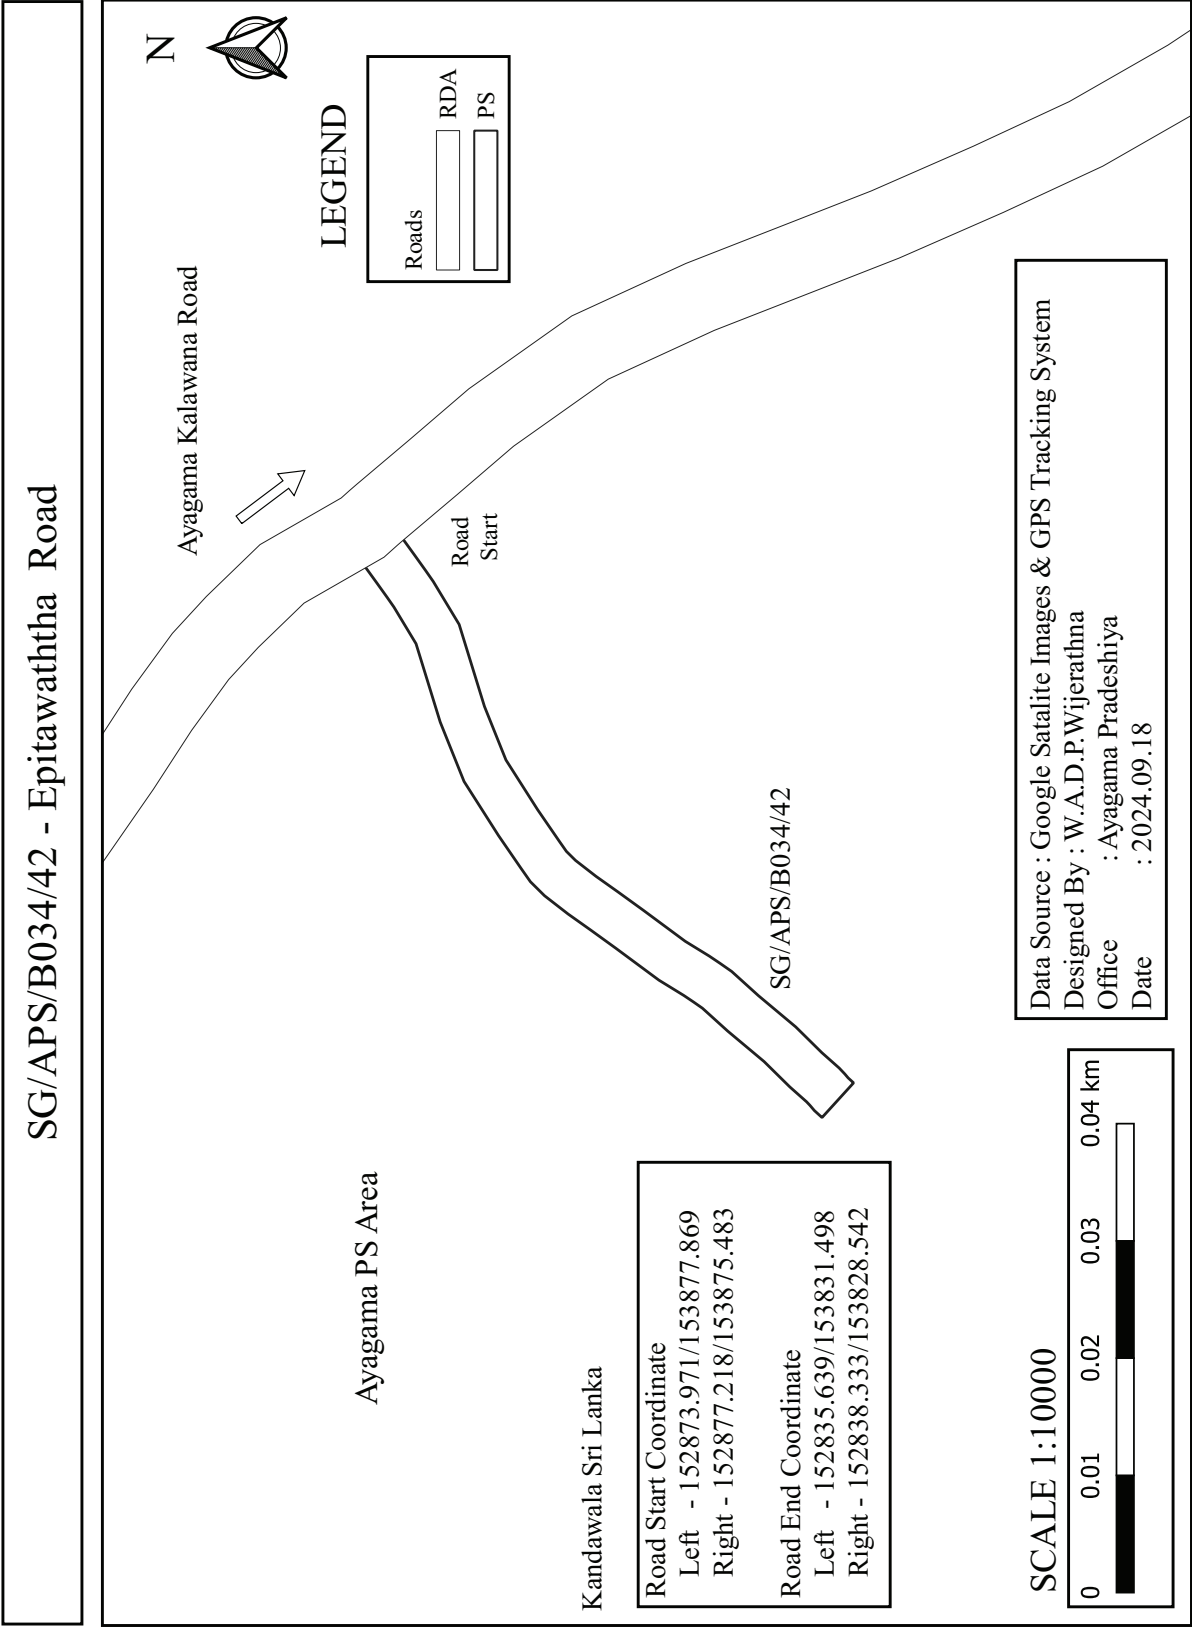





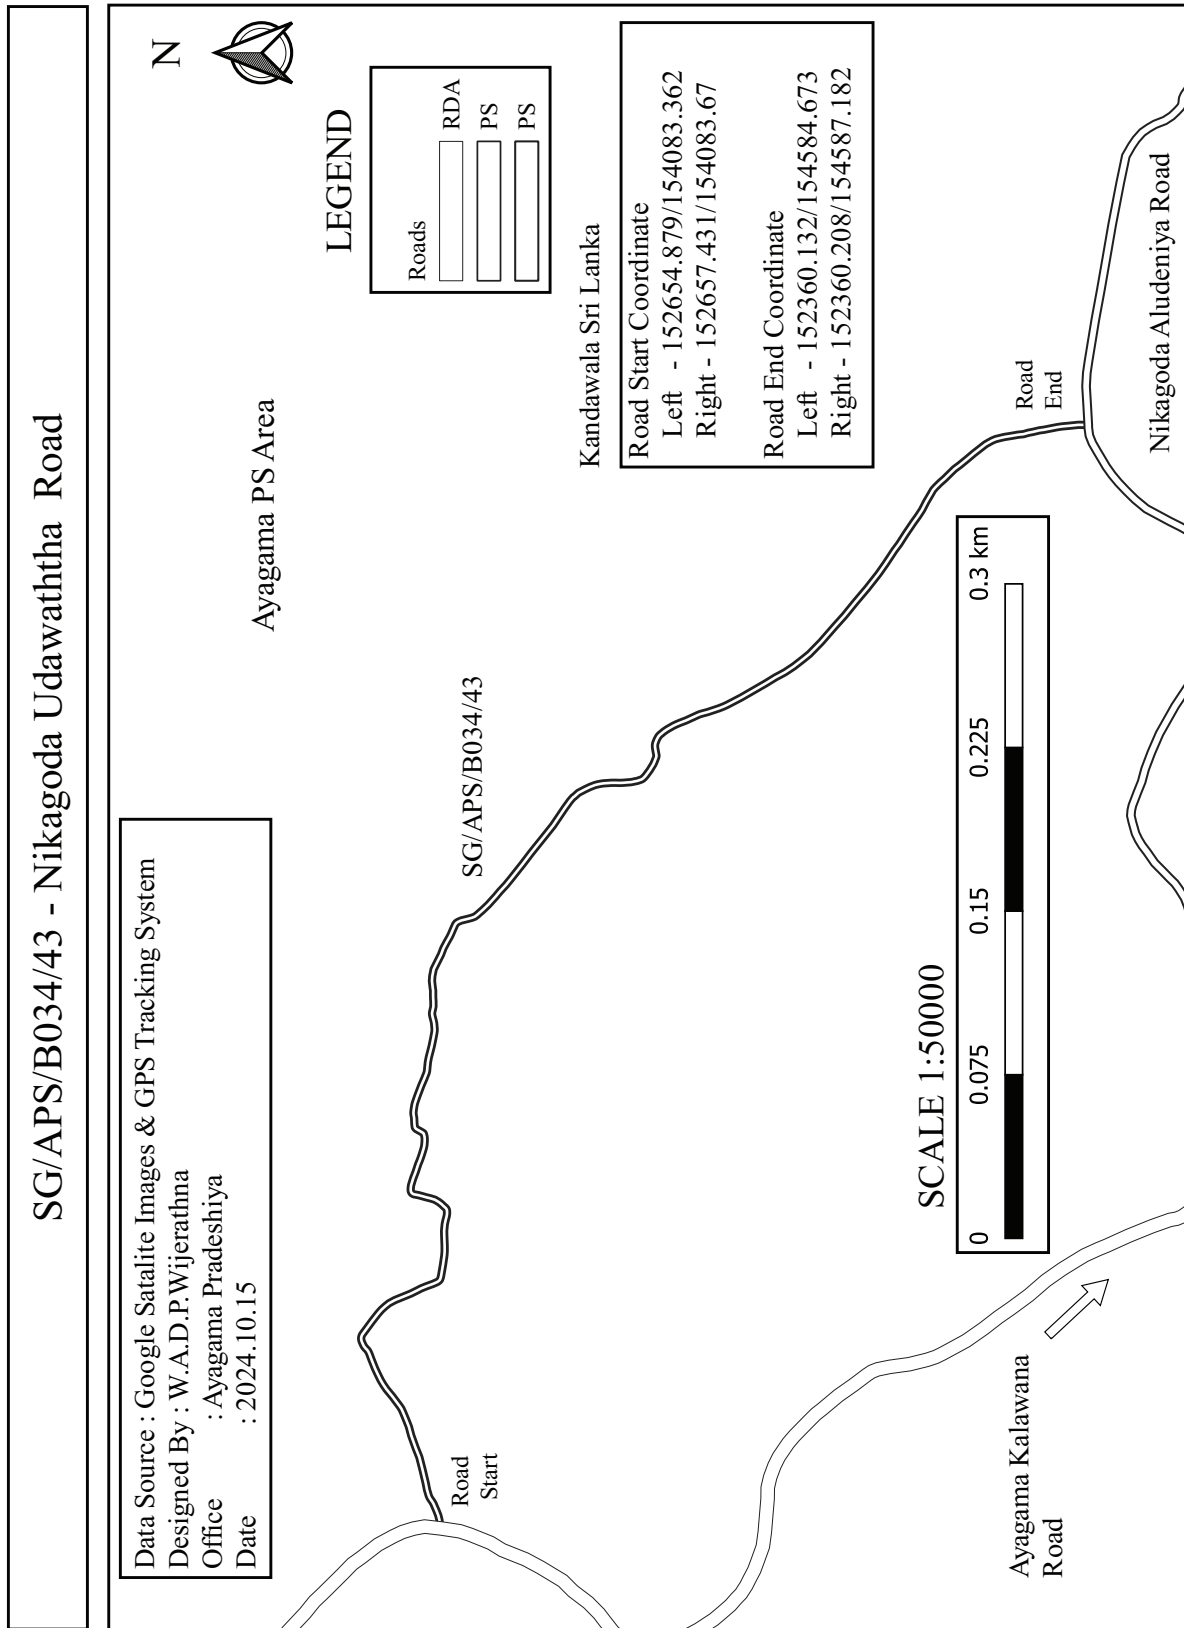


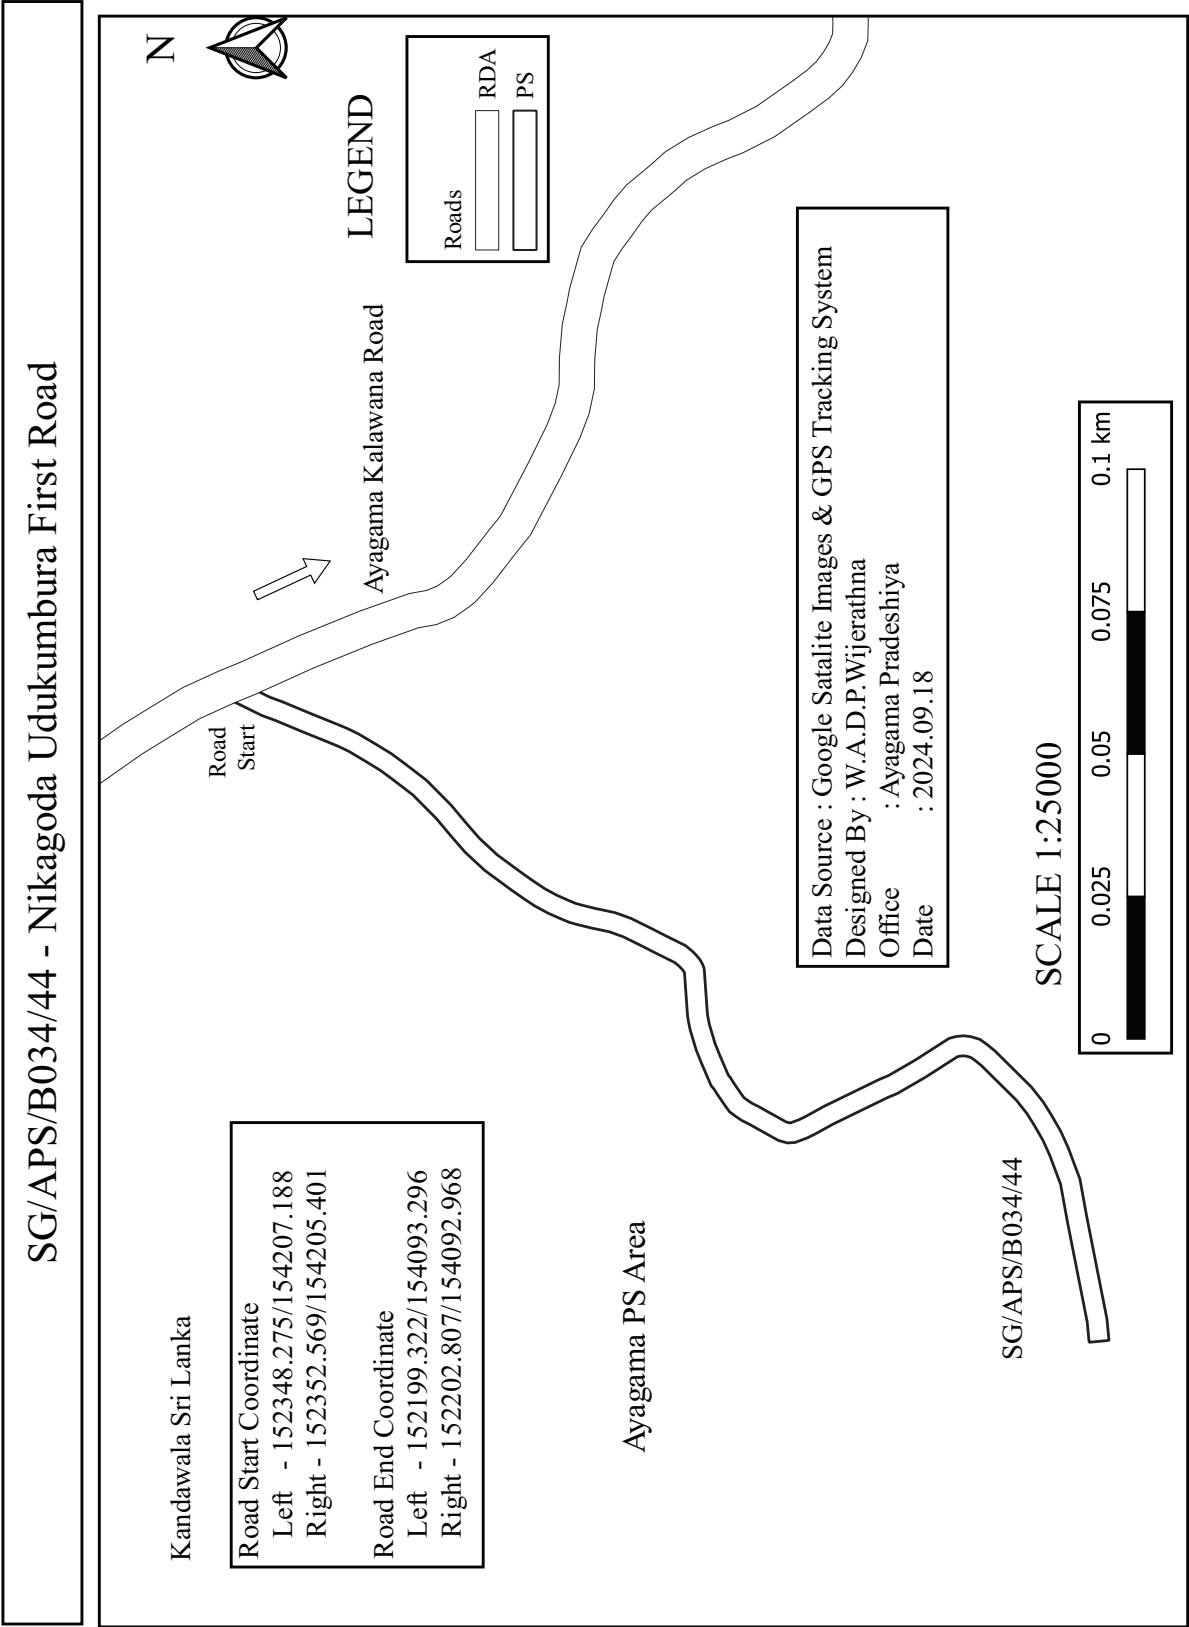


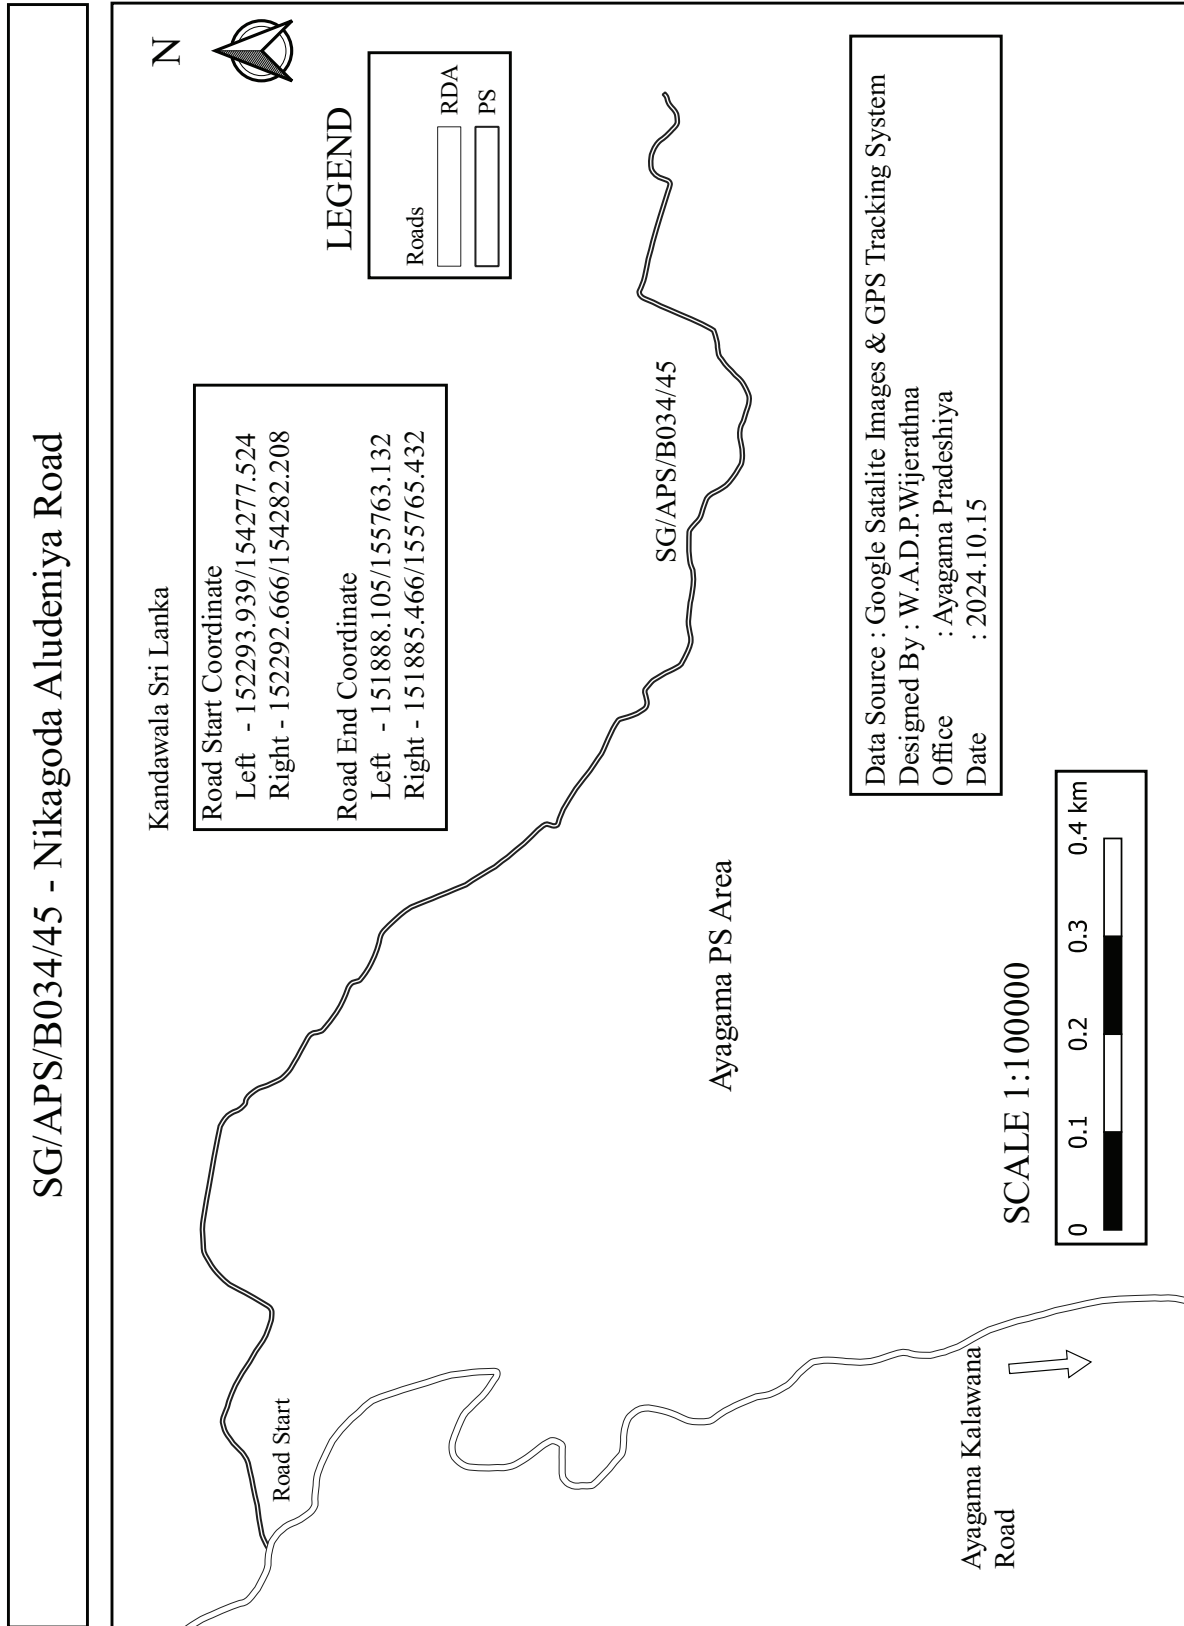


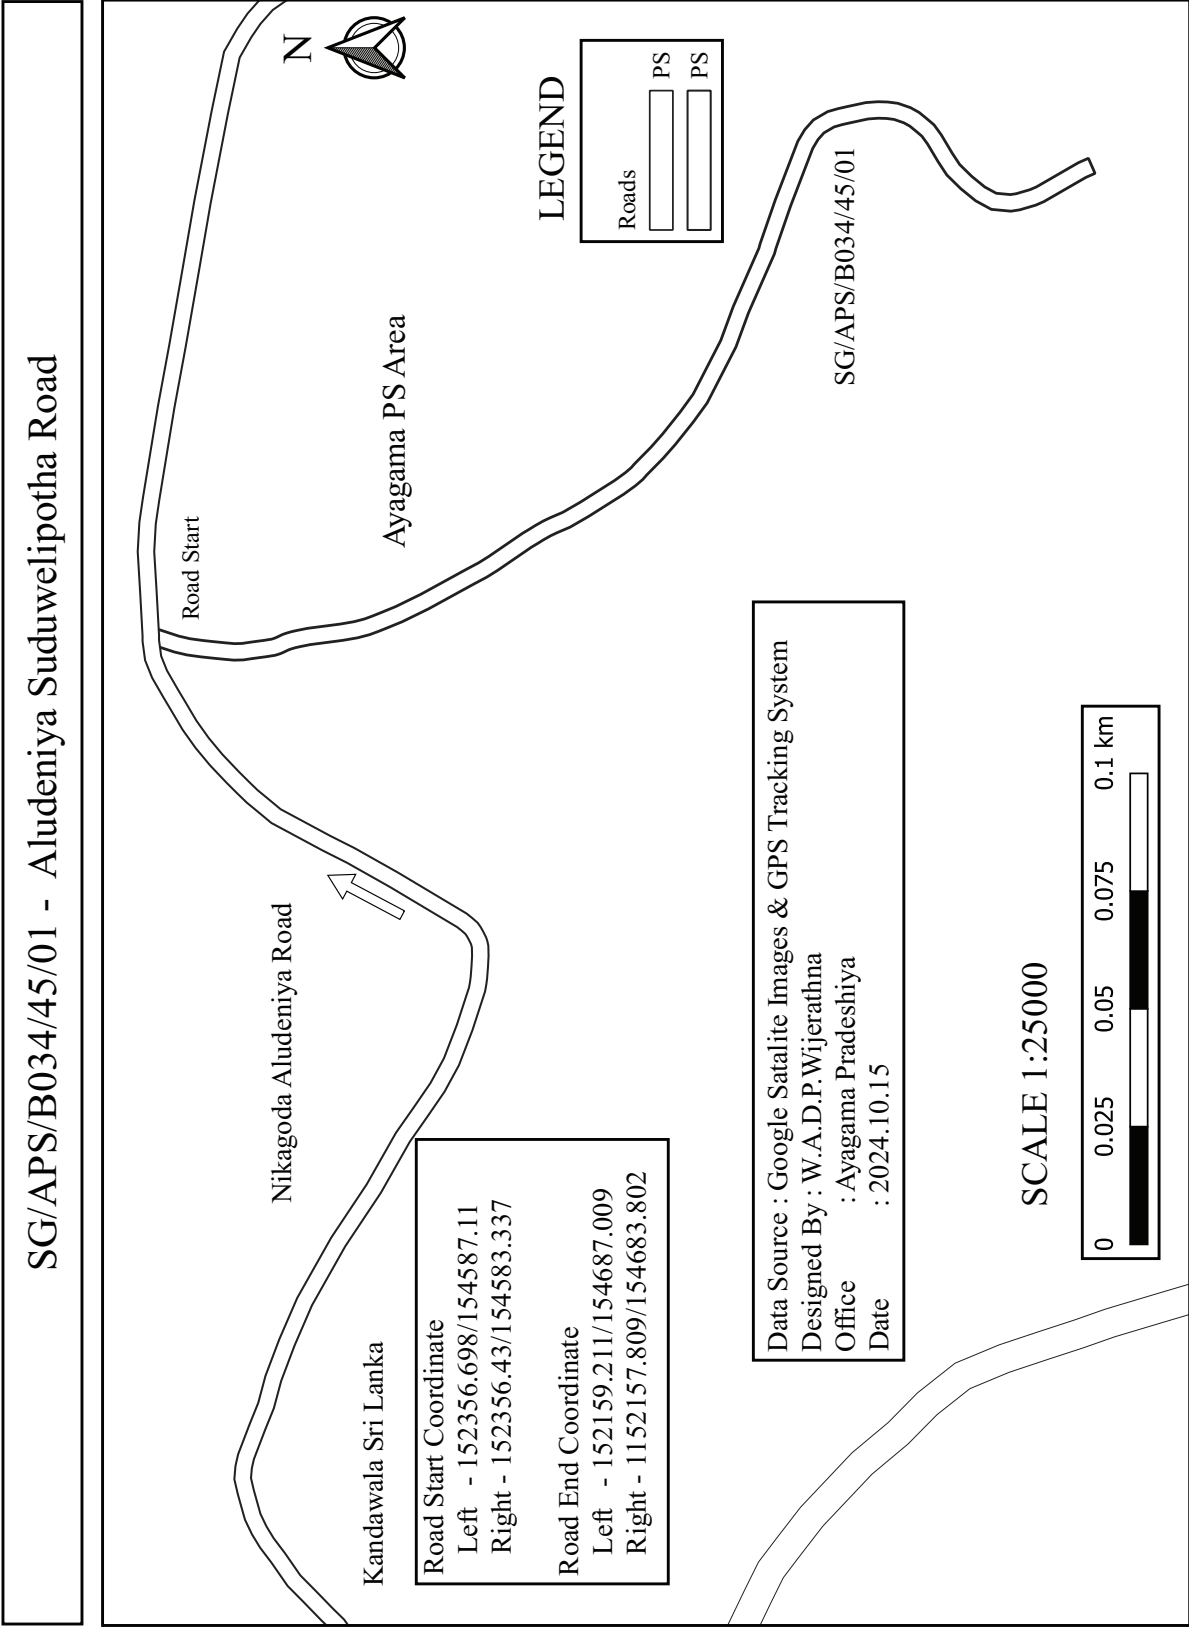

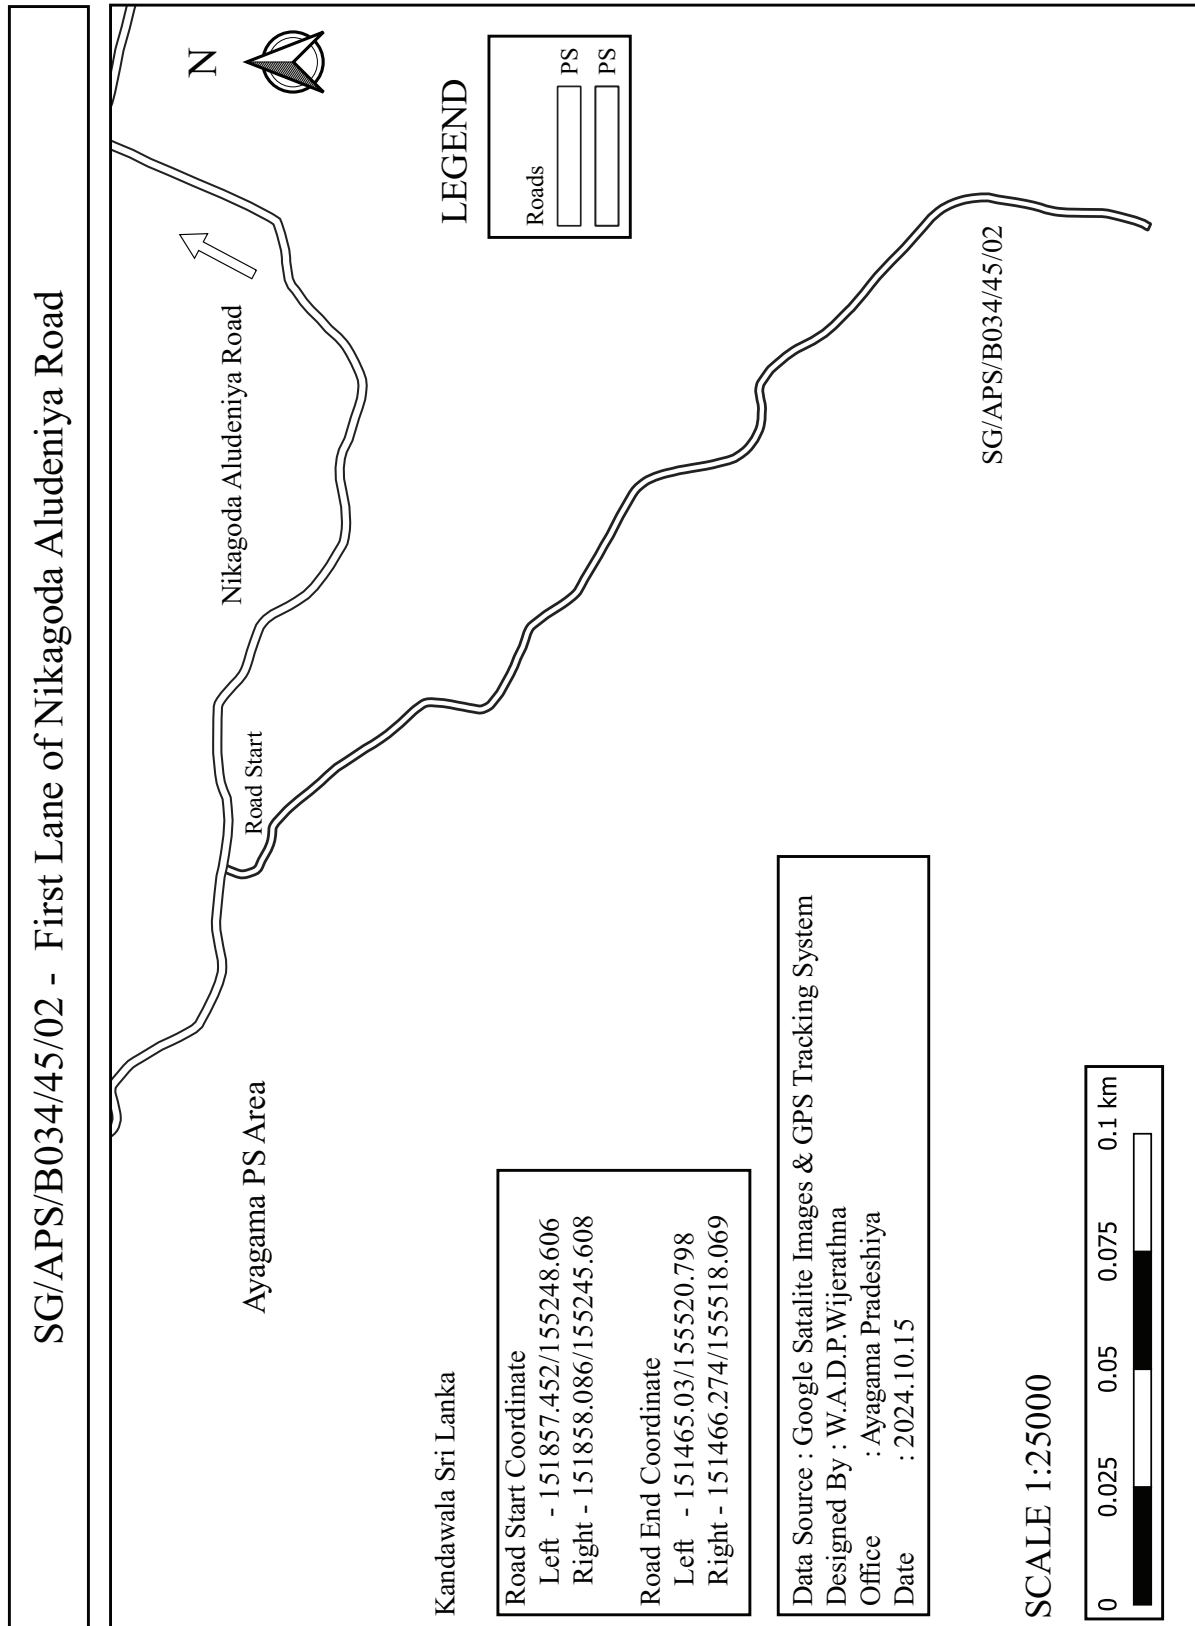


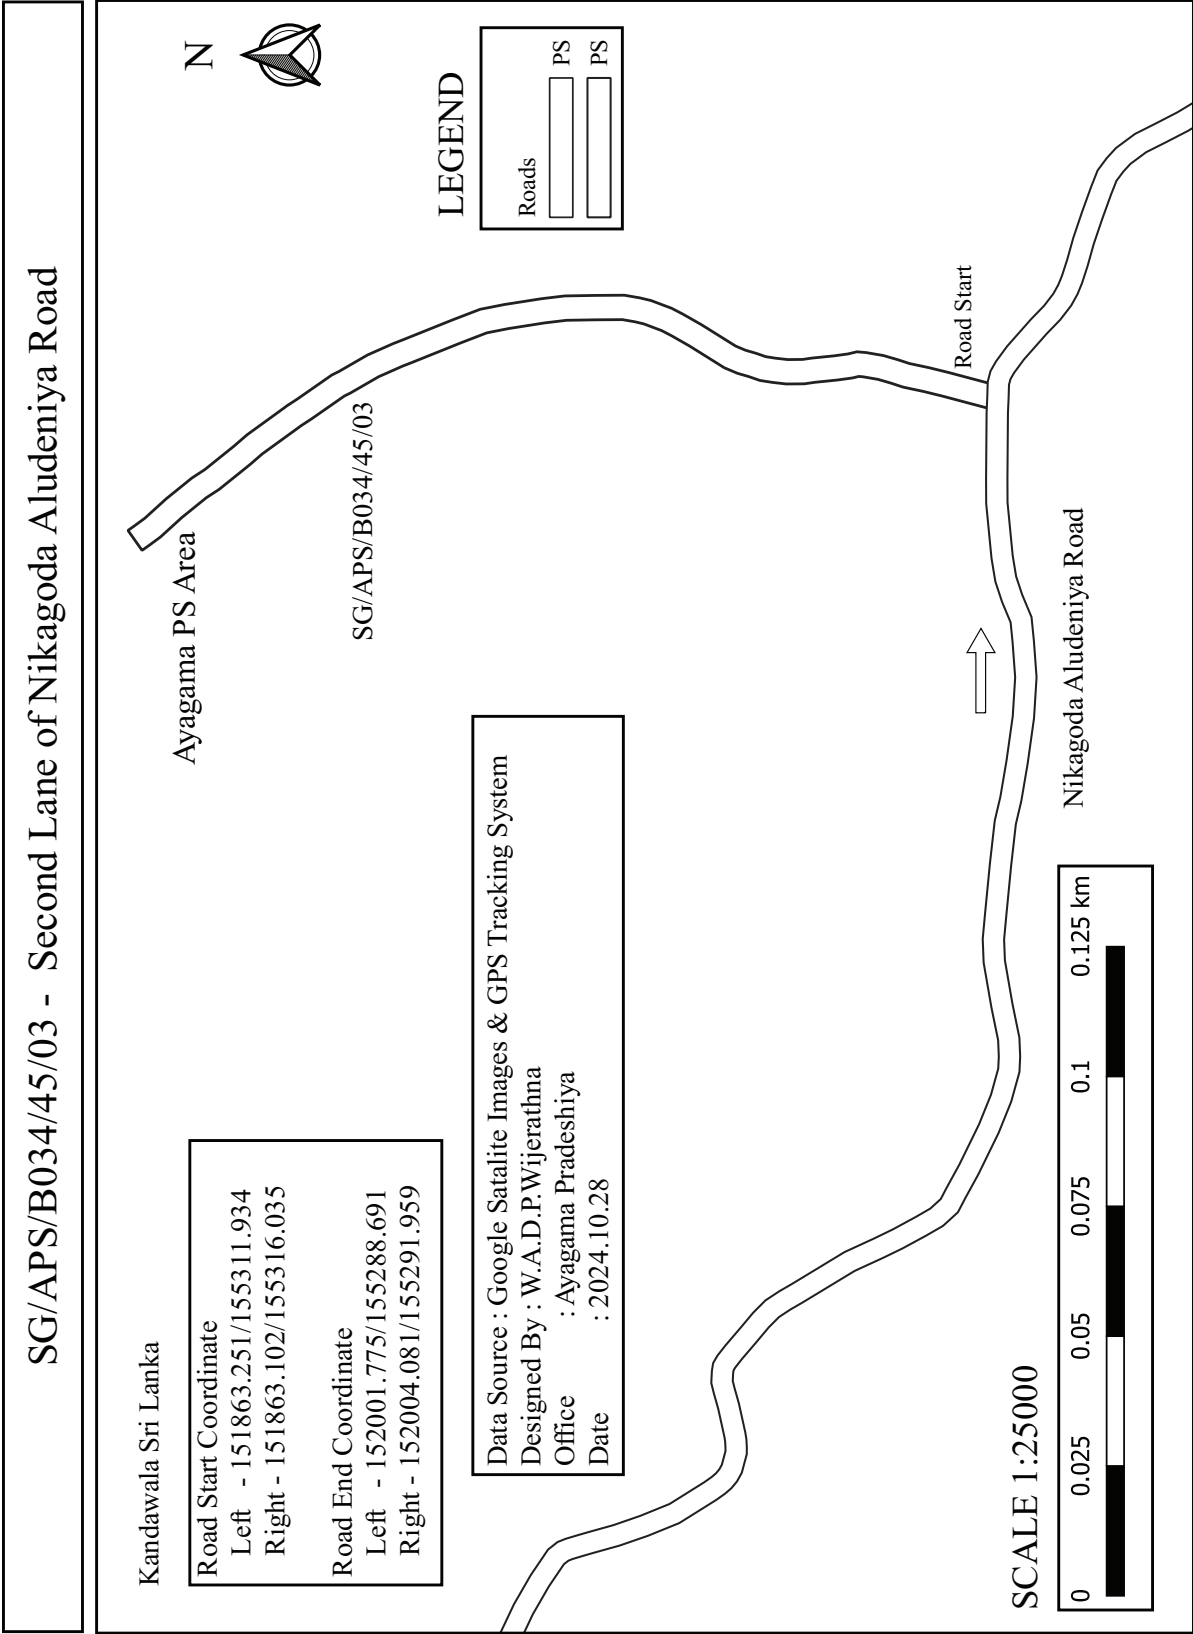


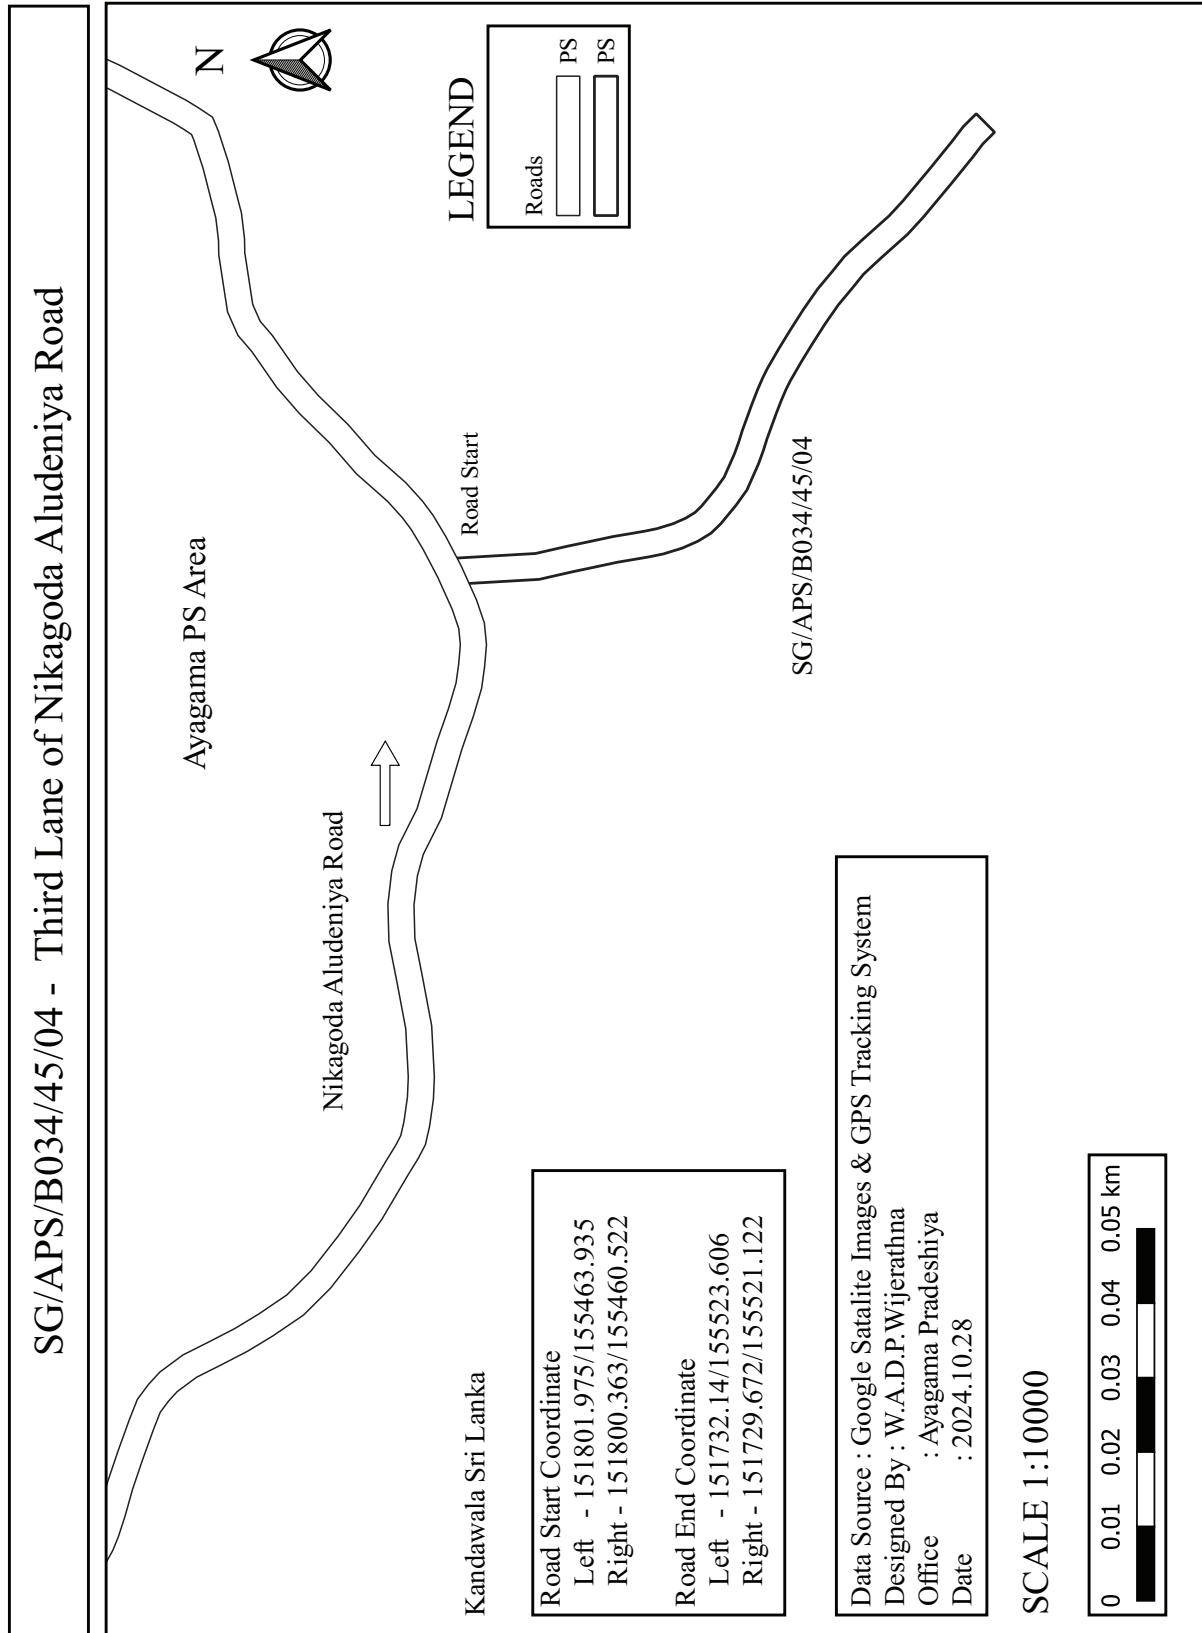

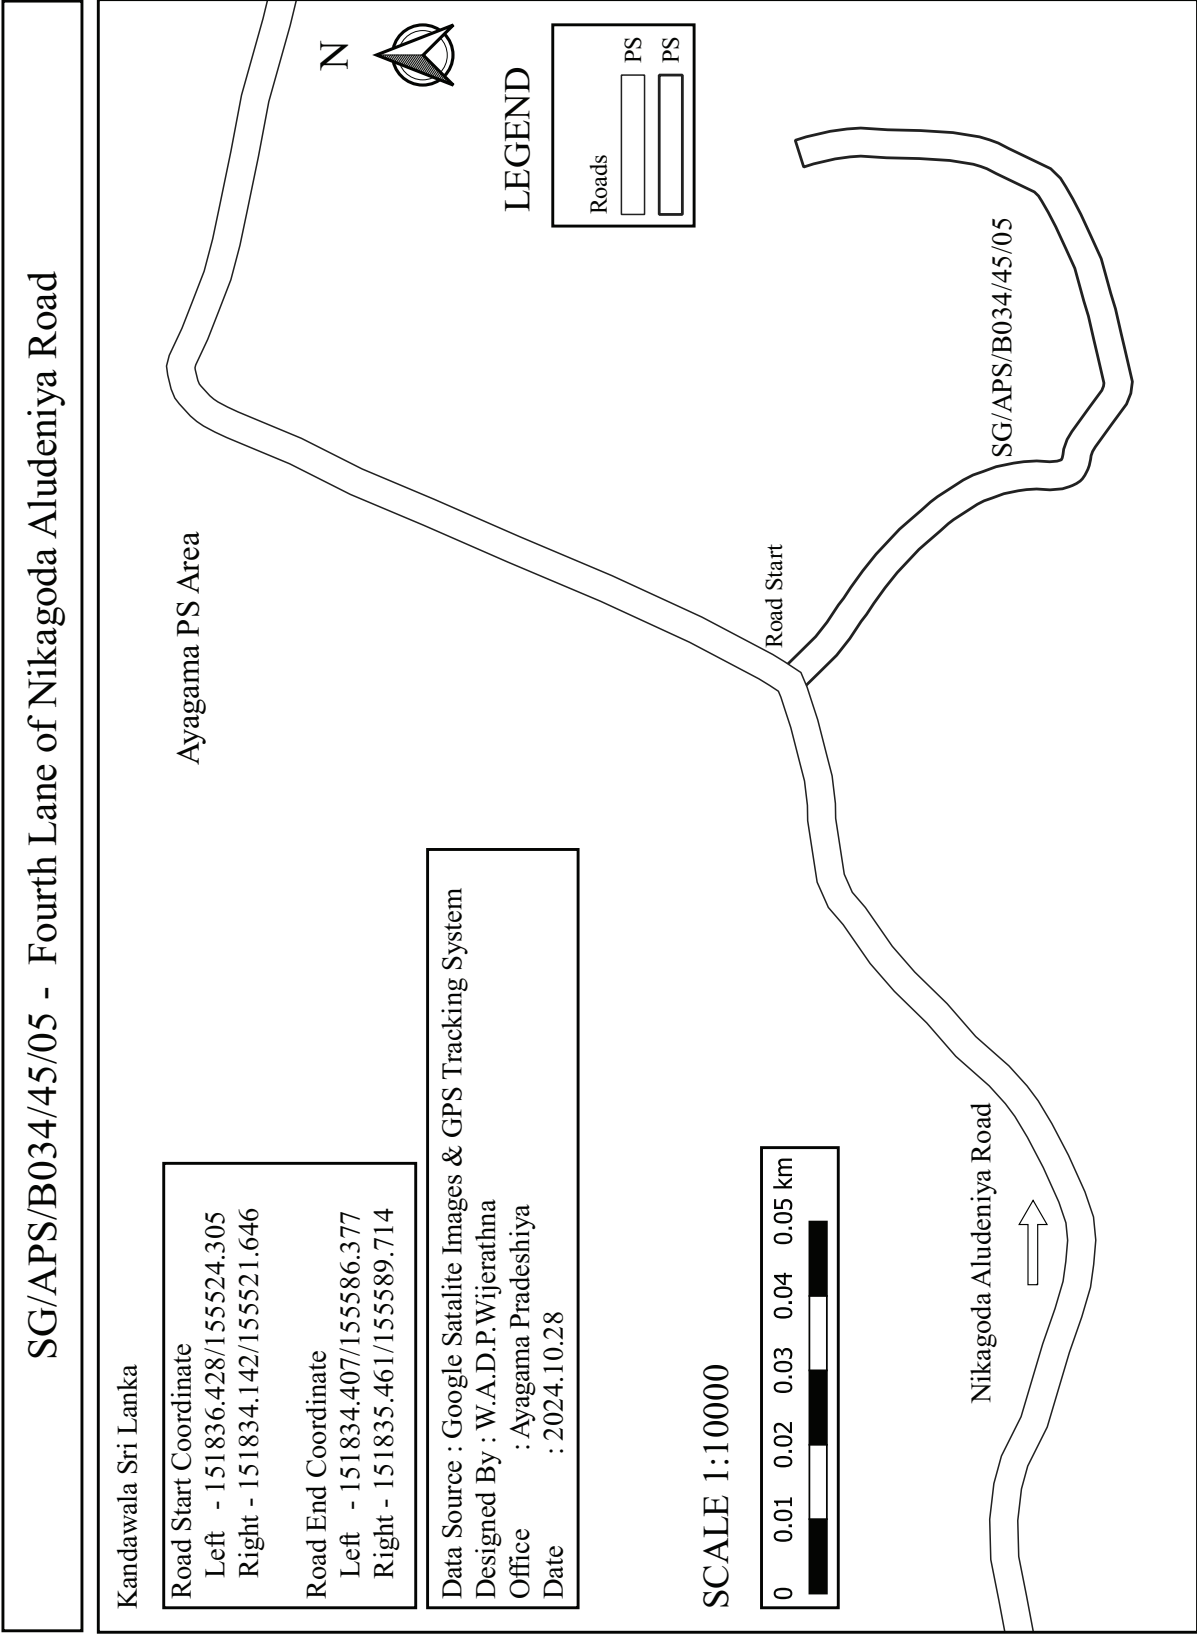



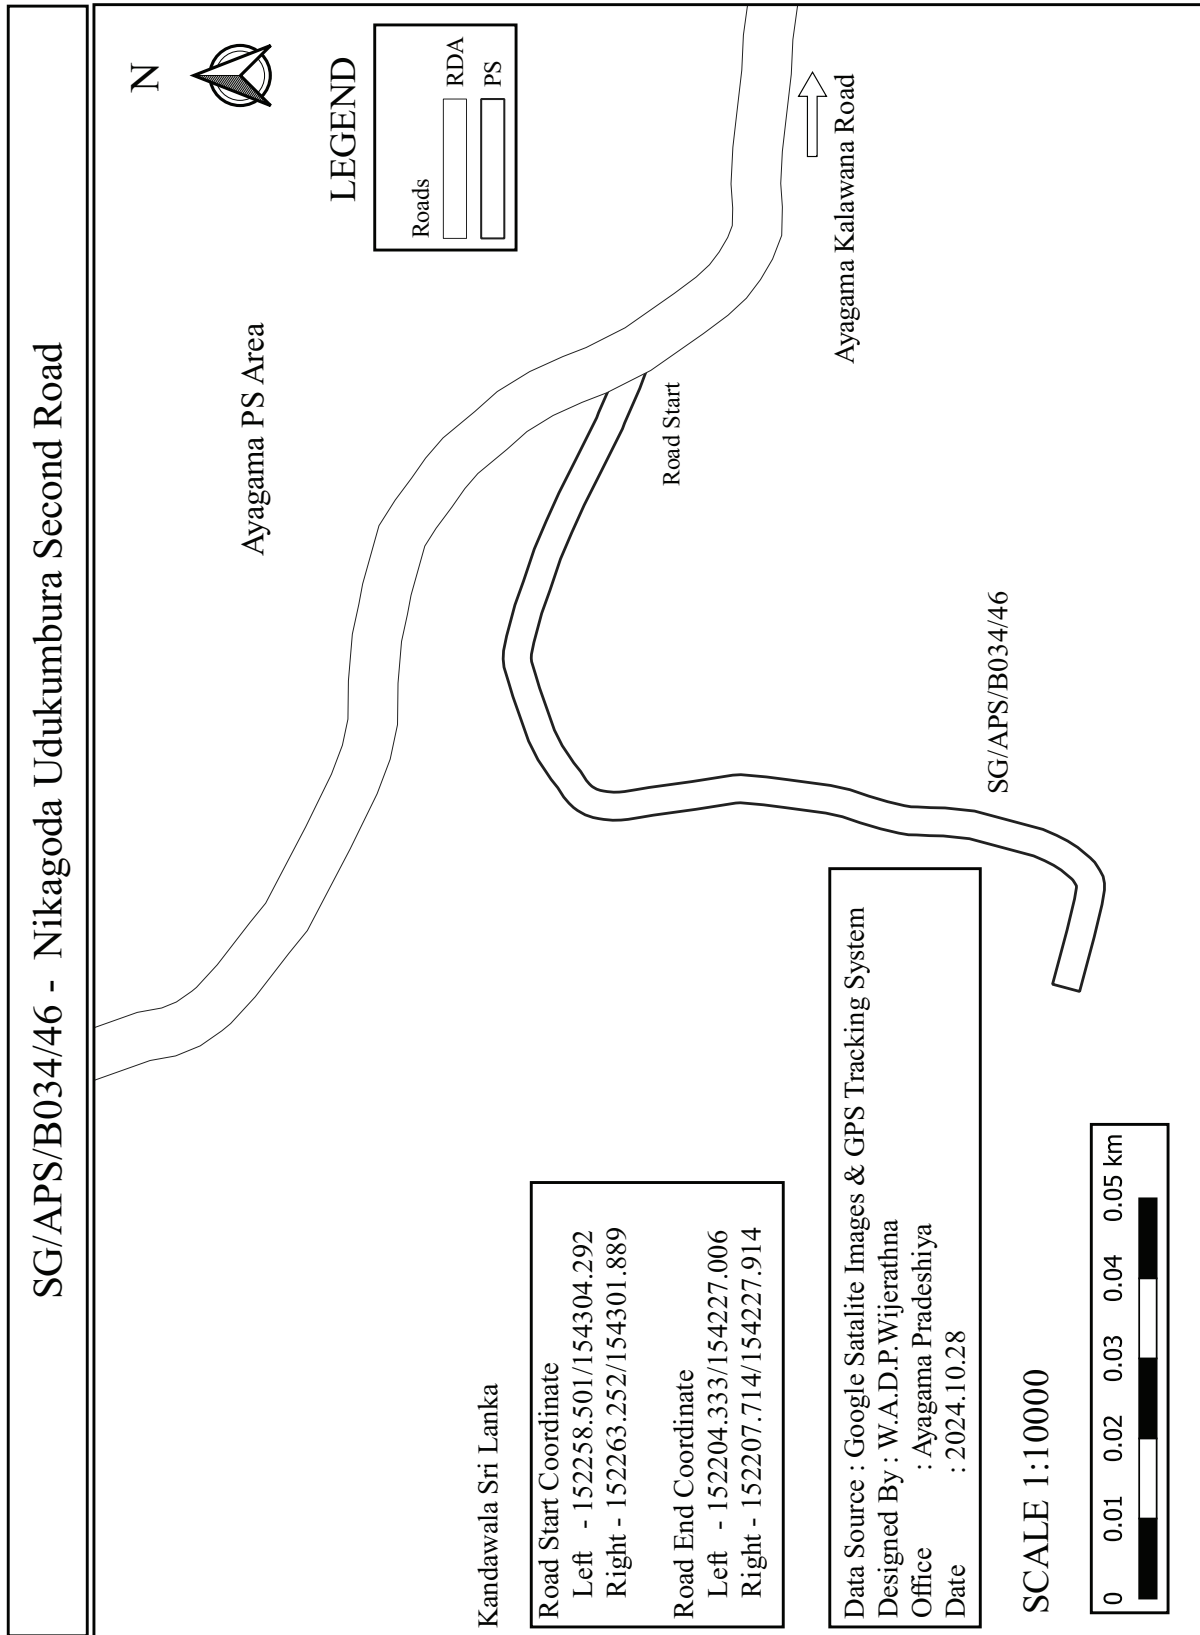

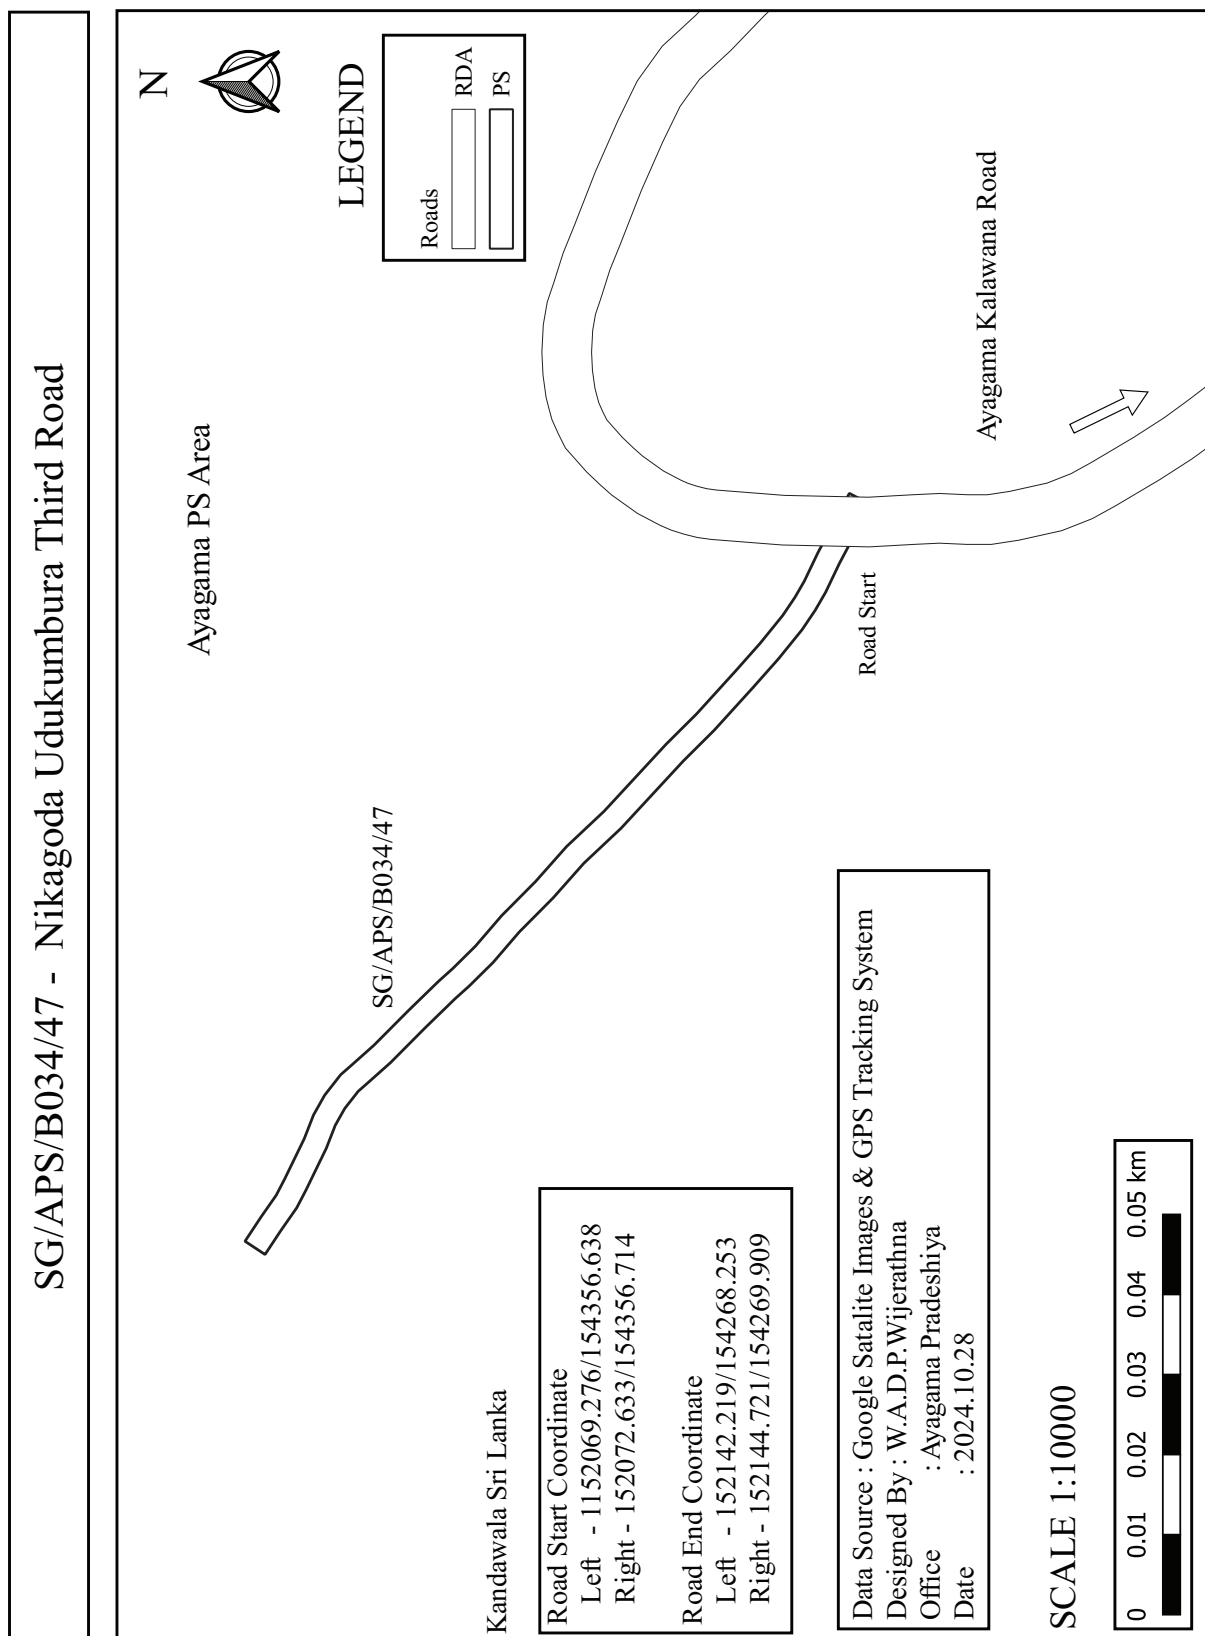

## Kandawala Sri Lanka

Road Start Coordinate

Left - 151954.285/154343.495

Right - 1151957.929/154340.37

Road End Coordinate

Left - 151929.476/154249.566

Right - 151930.281/154252.456

Data Source : Google Satalite Images & GPS Tracking System

Designed By : W.A.D.P.Wijerathna

Office : Ayagama Pradeshiya

Date : 2024.10.28



## LEGEND

## Roads

□ RDA

PS


2


Ayagama Kalawana Road

## Road Start


SG/APS/B034/48


SCALE 1:10000

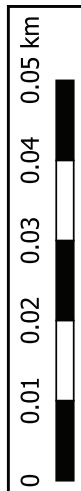


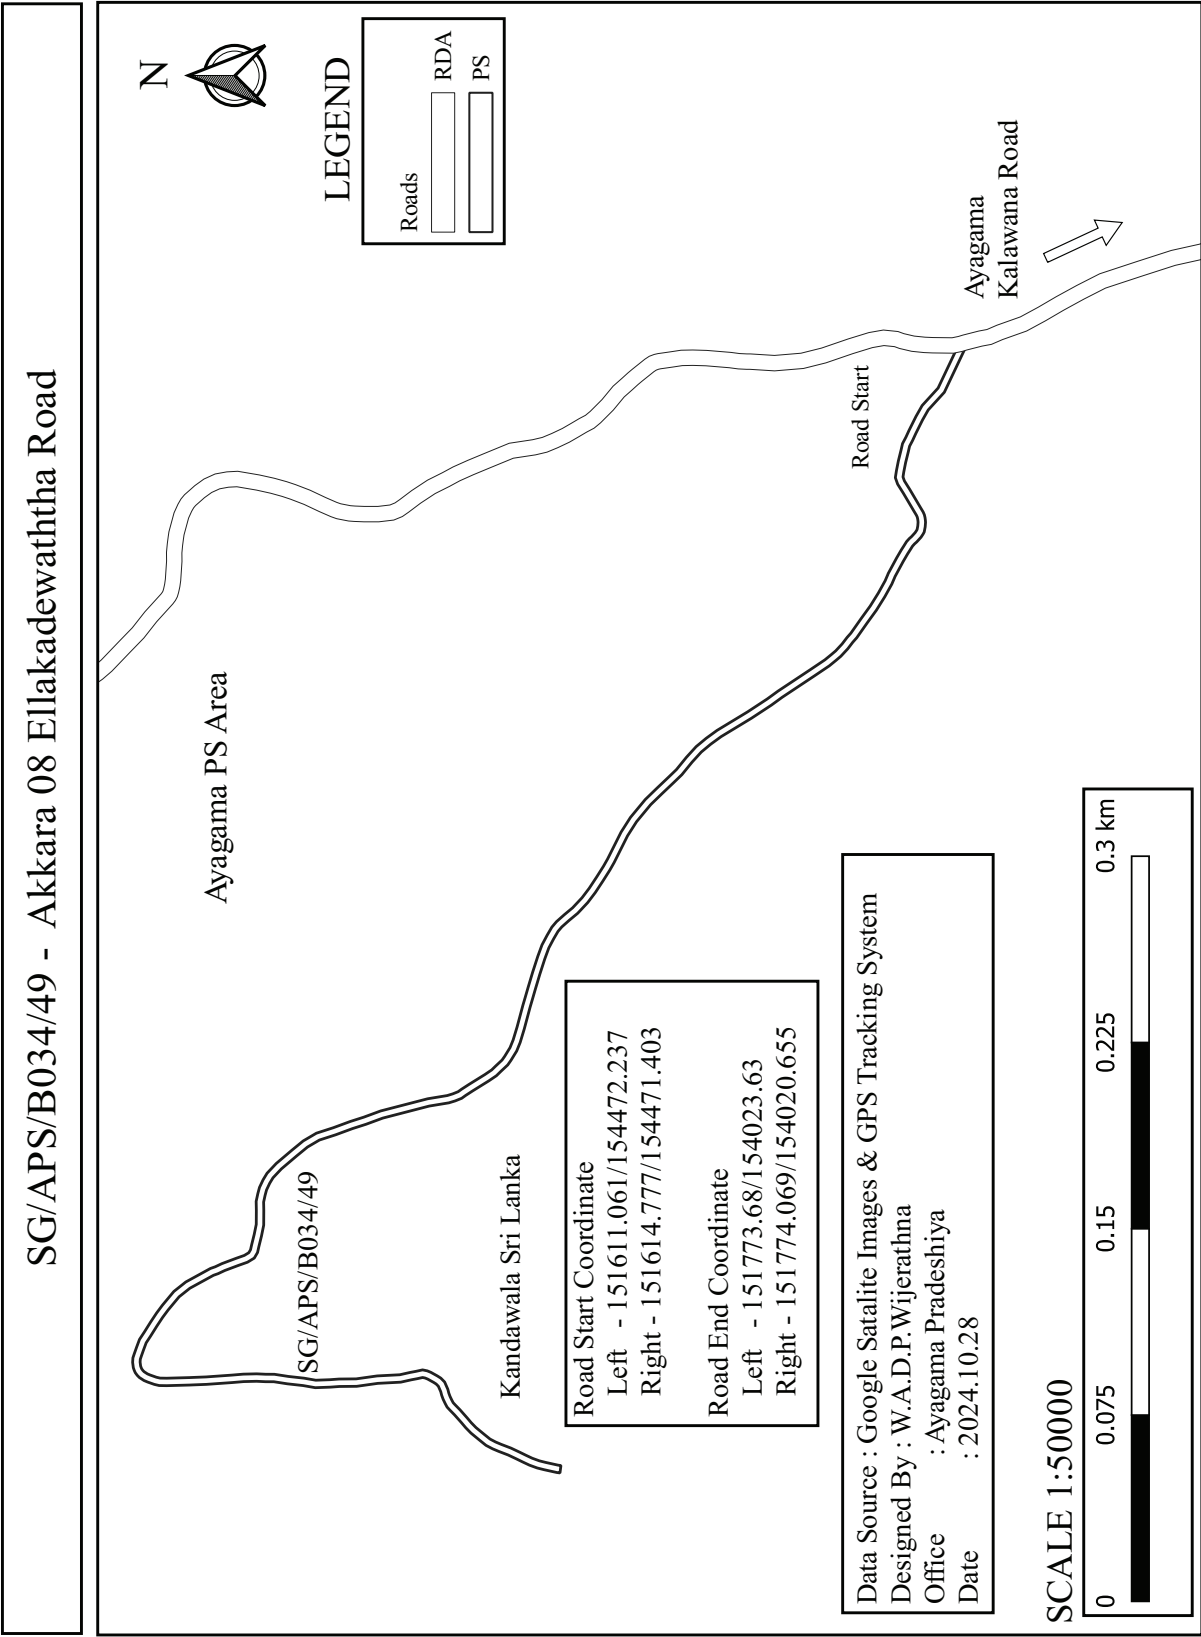


# SG/APS/B034/49/01 - Akkara 05 Imbulahithena Road

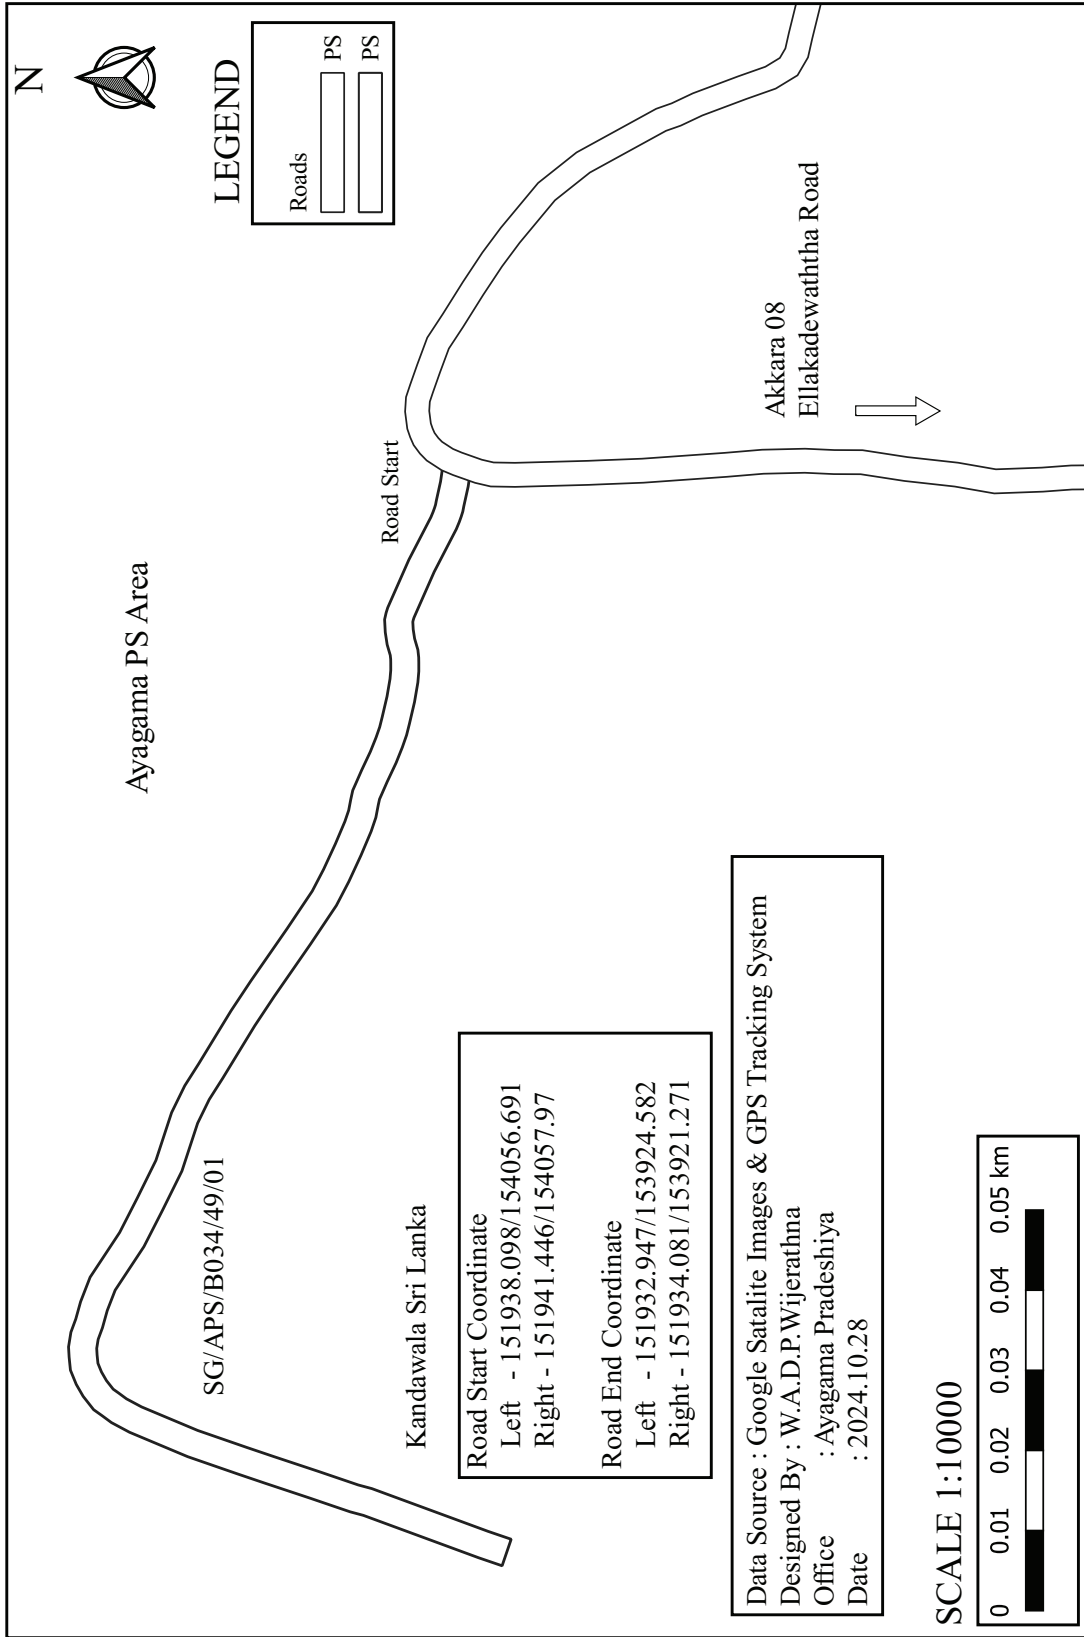


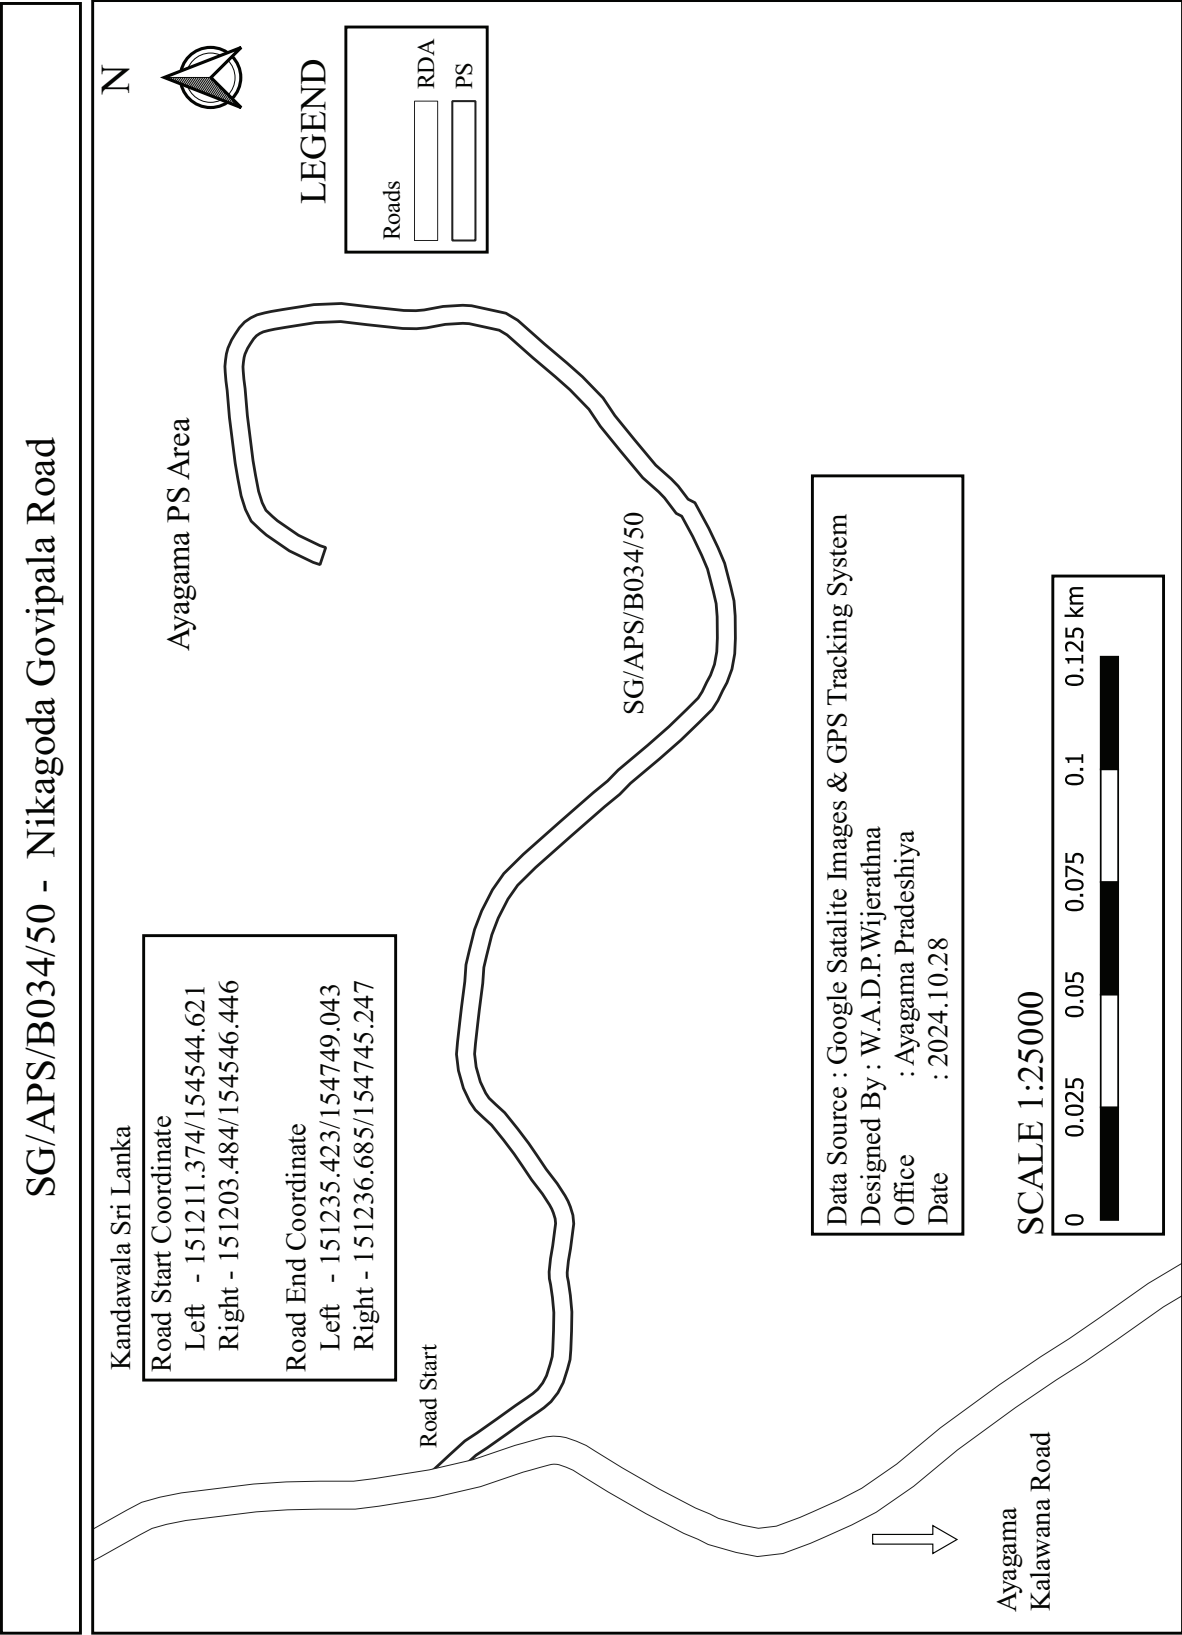


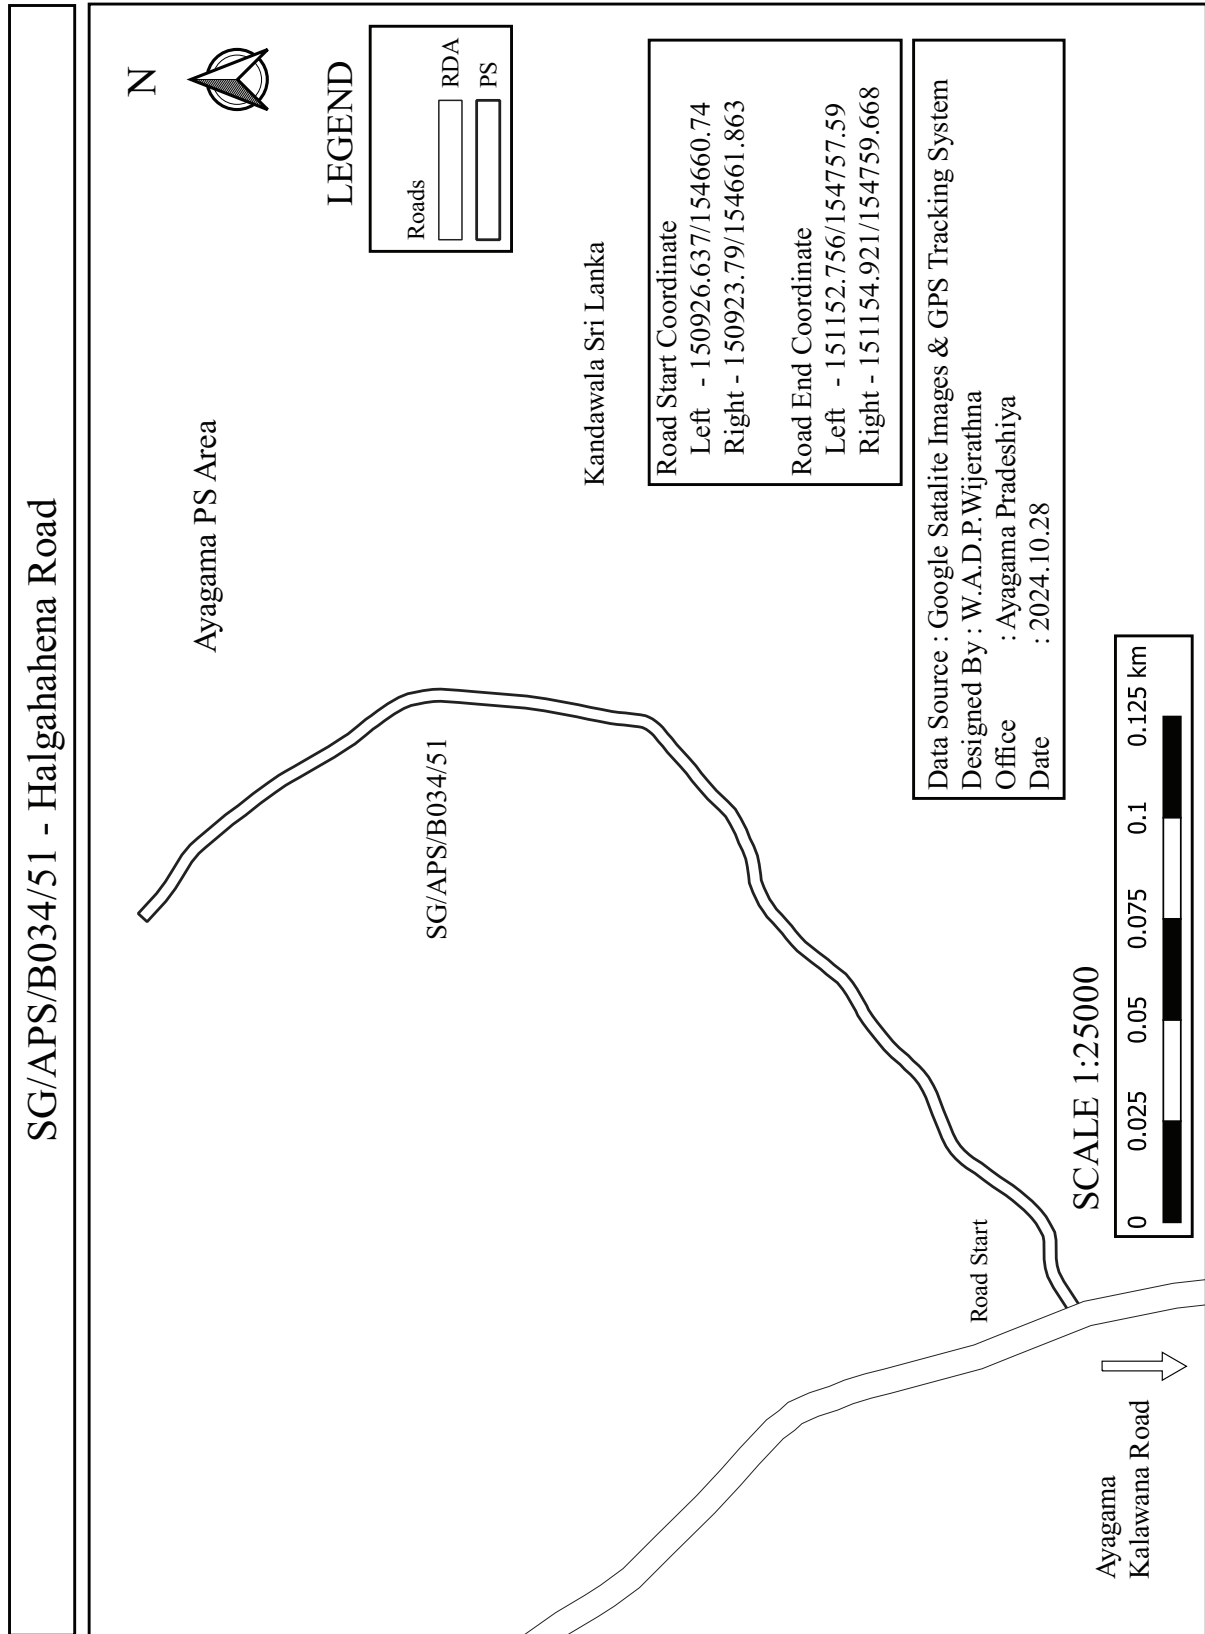


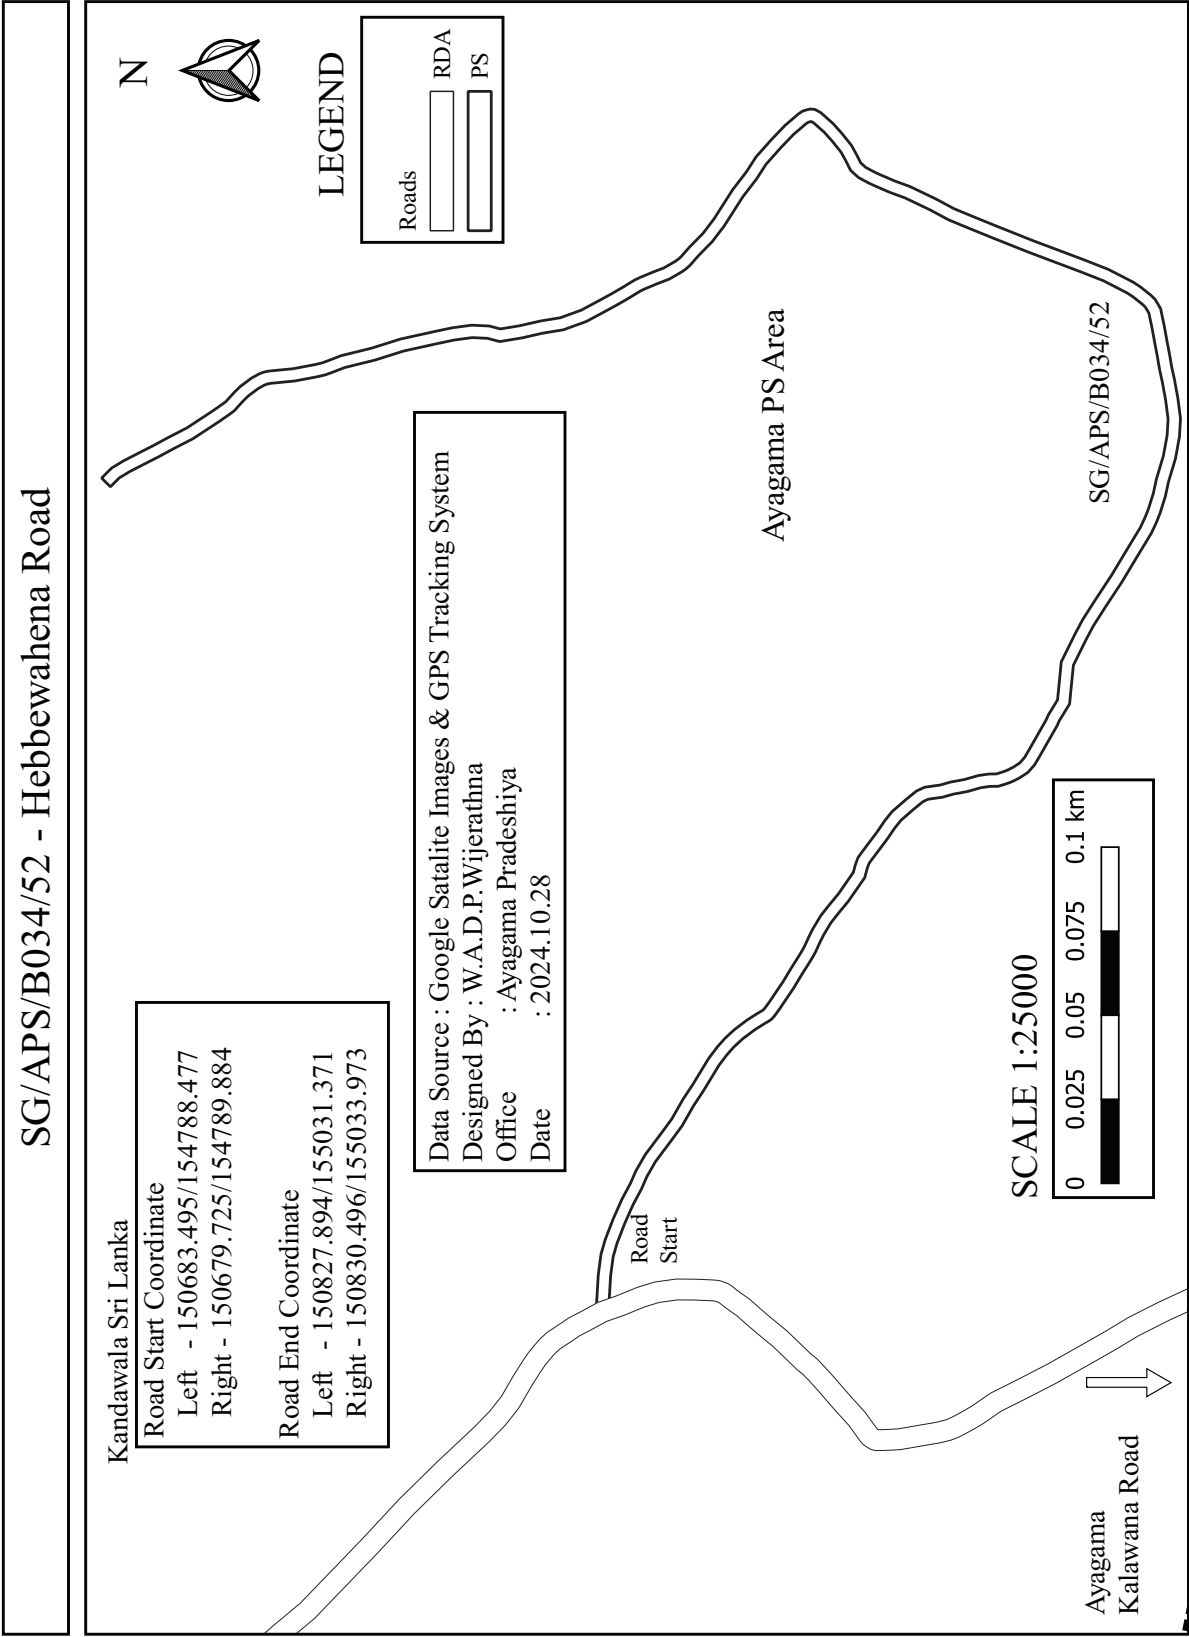





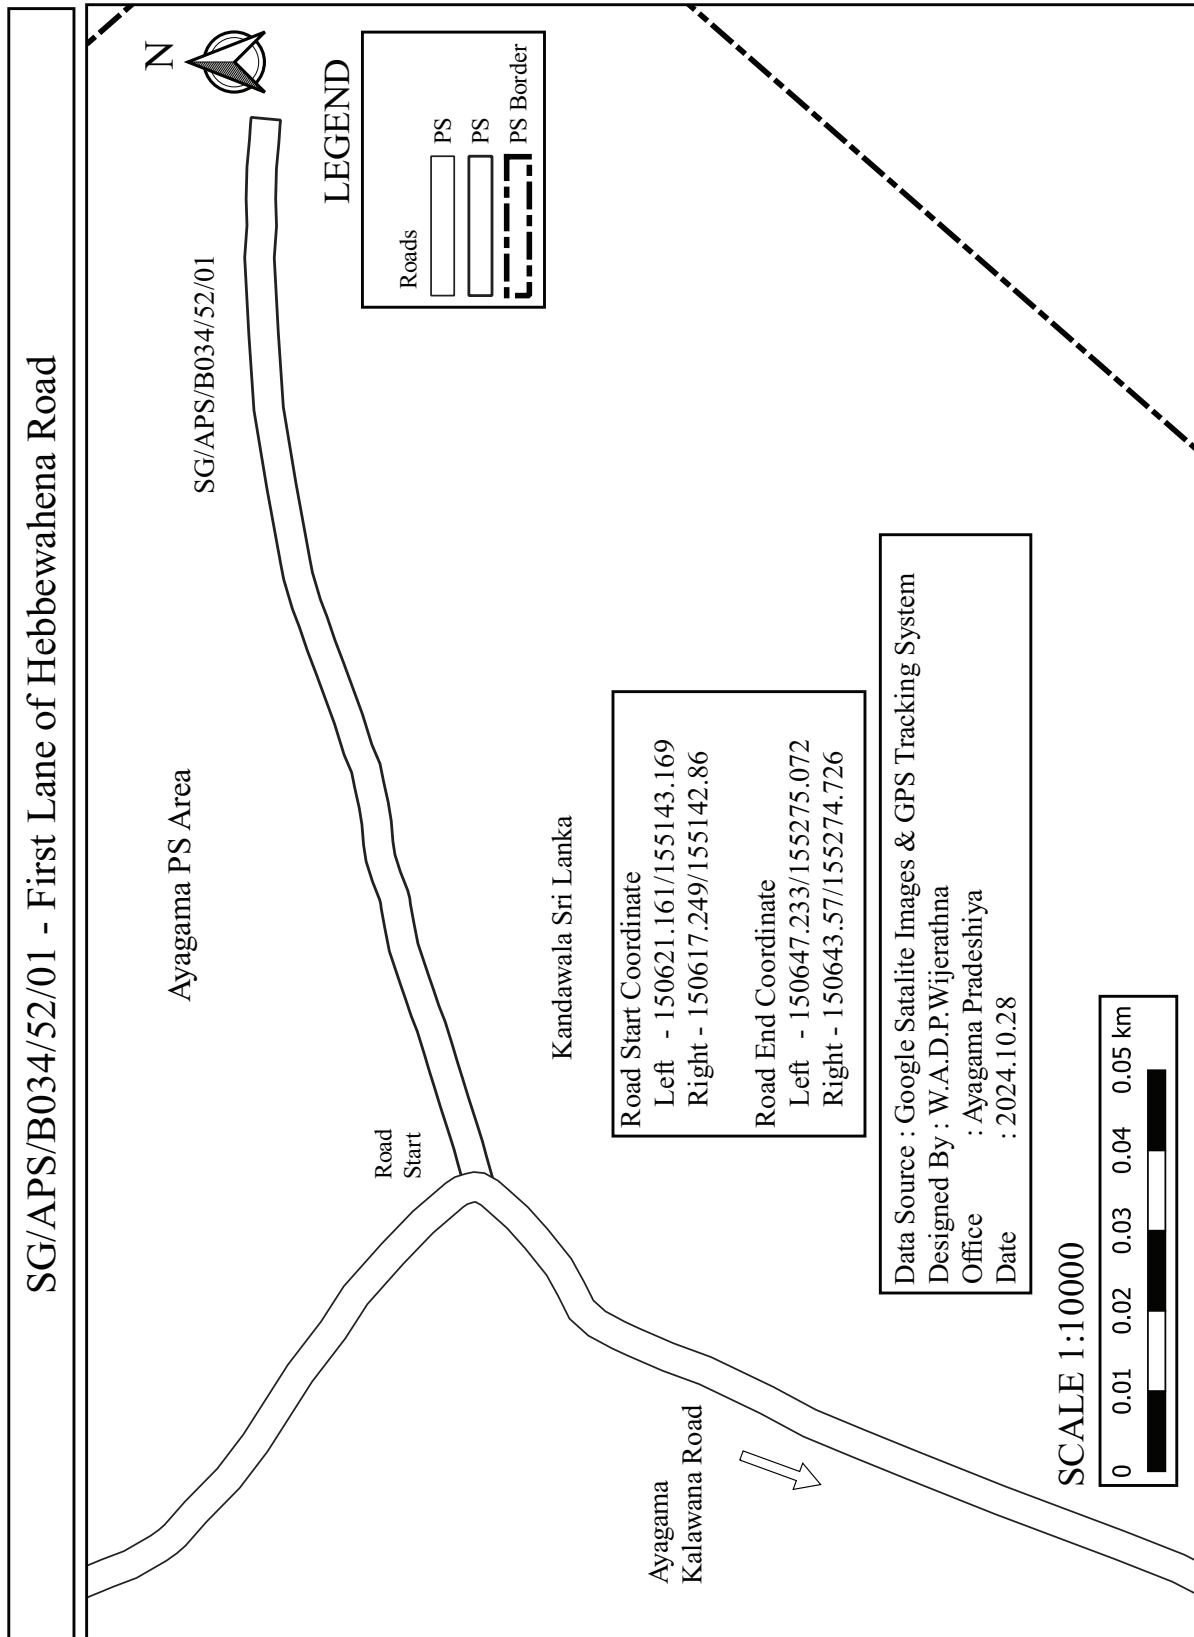


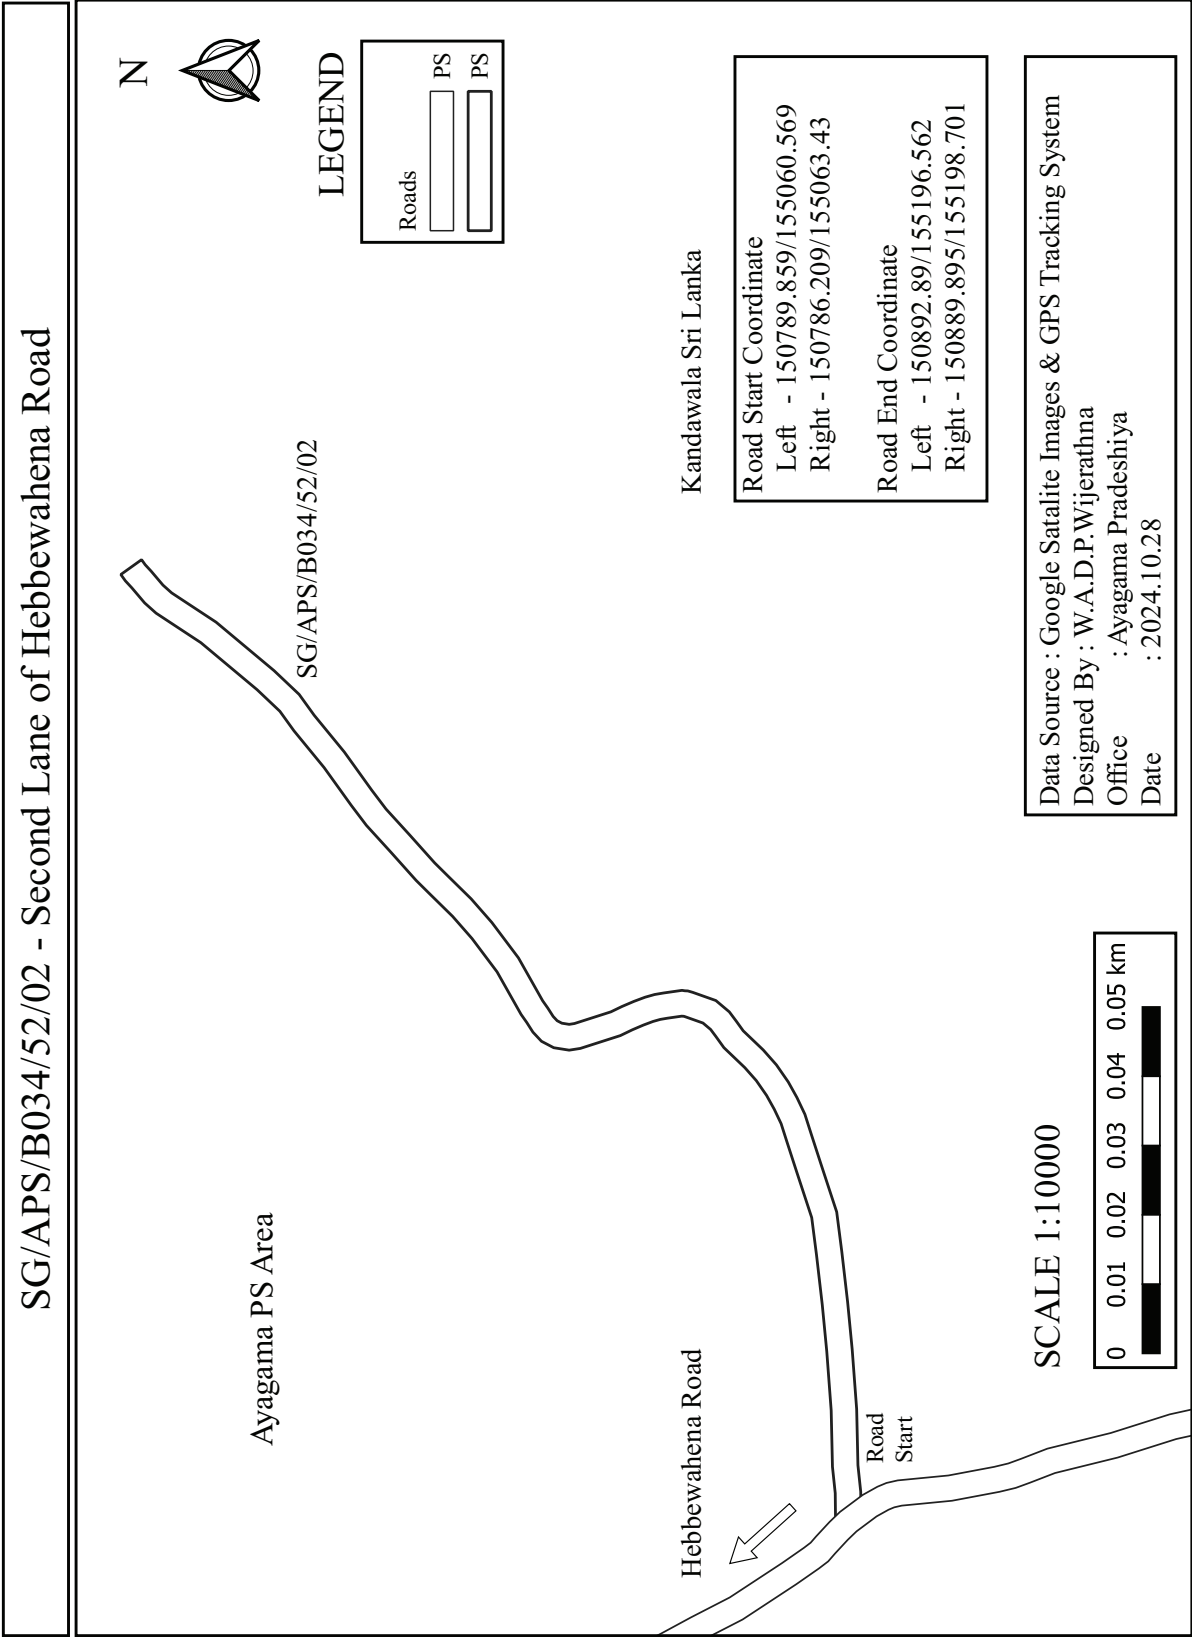


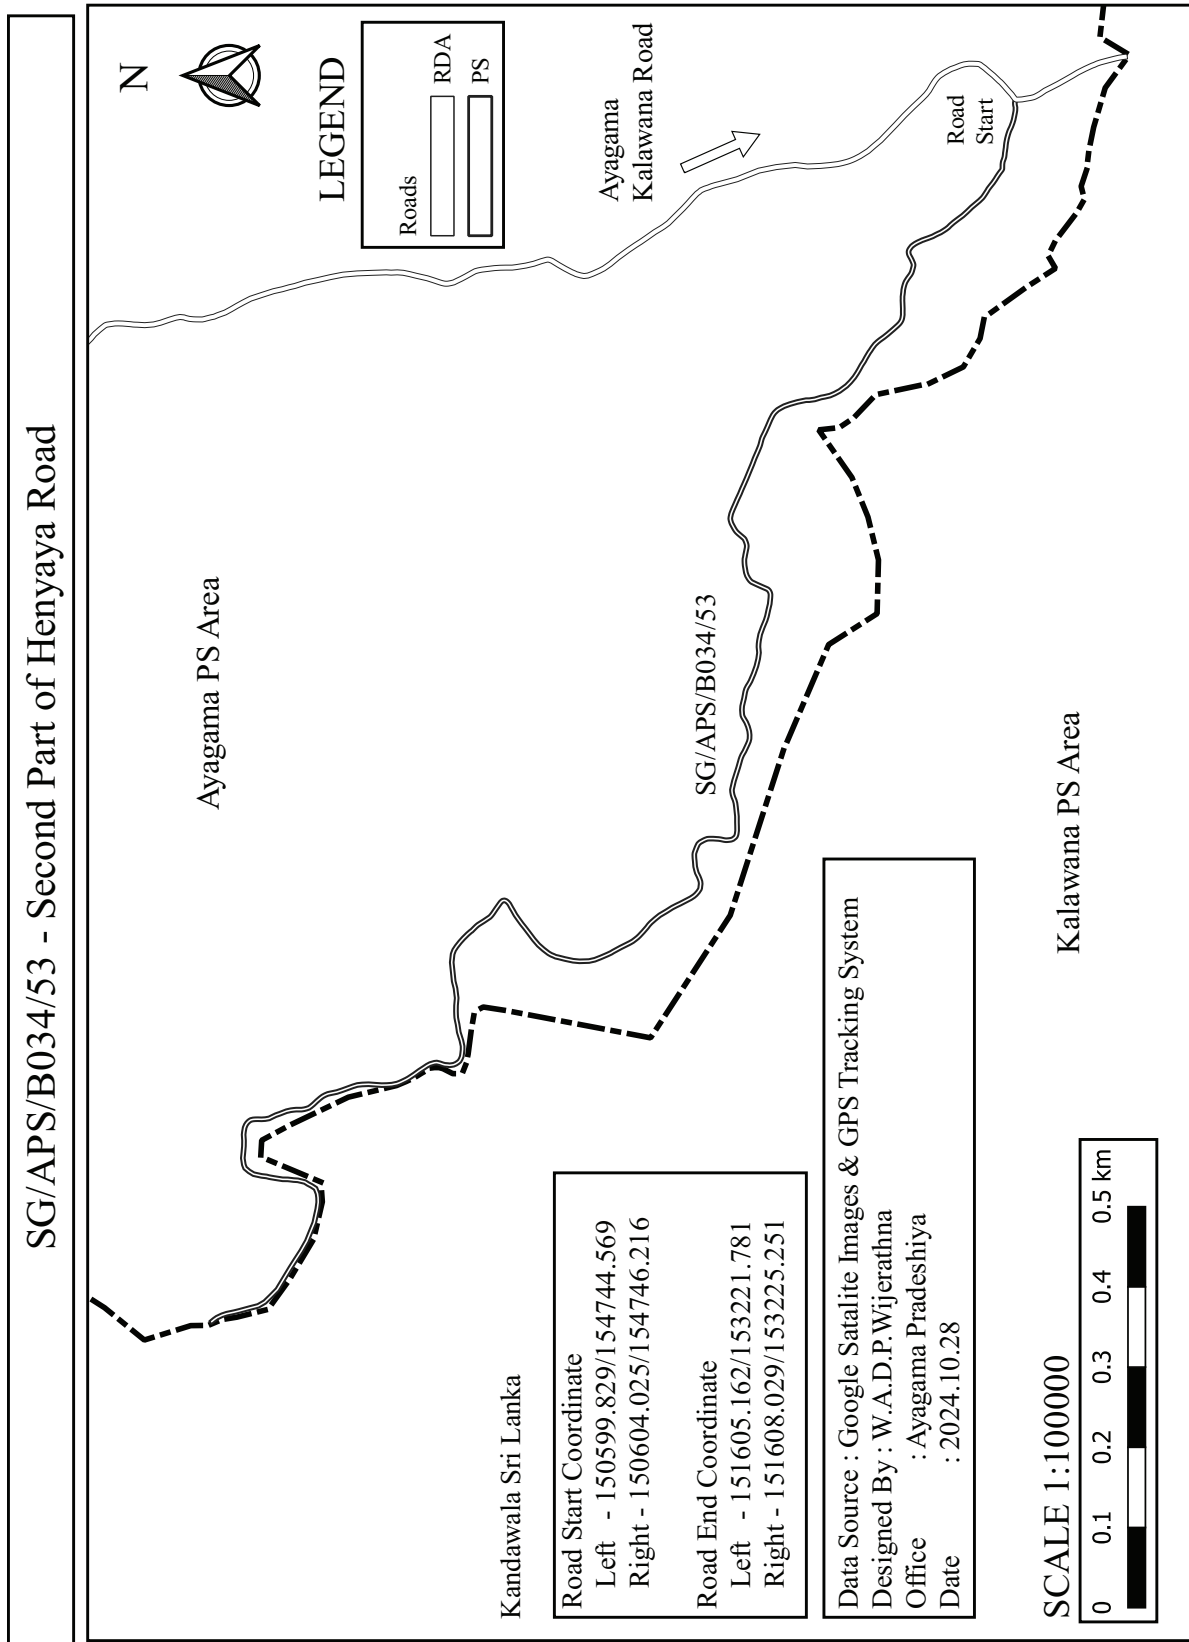


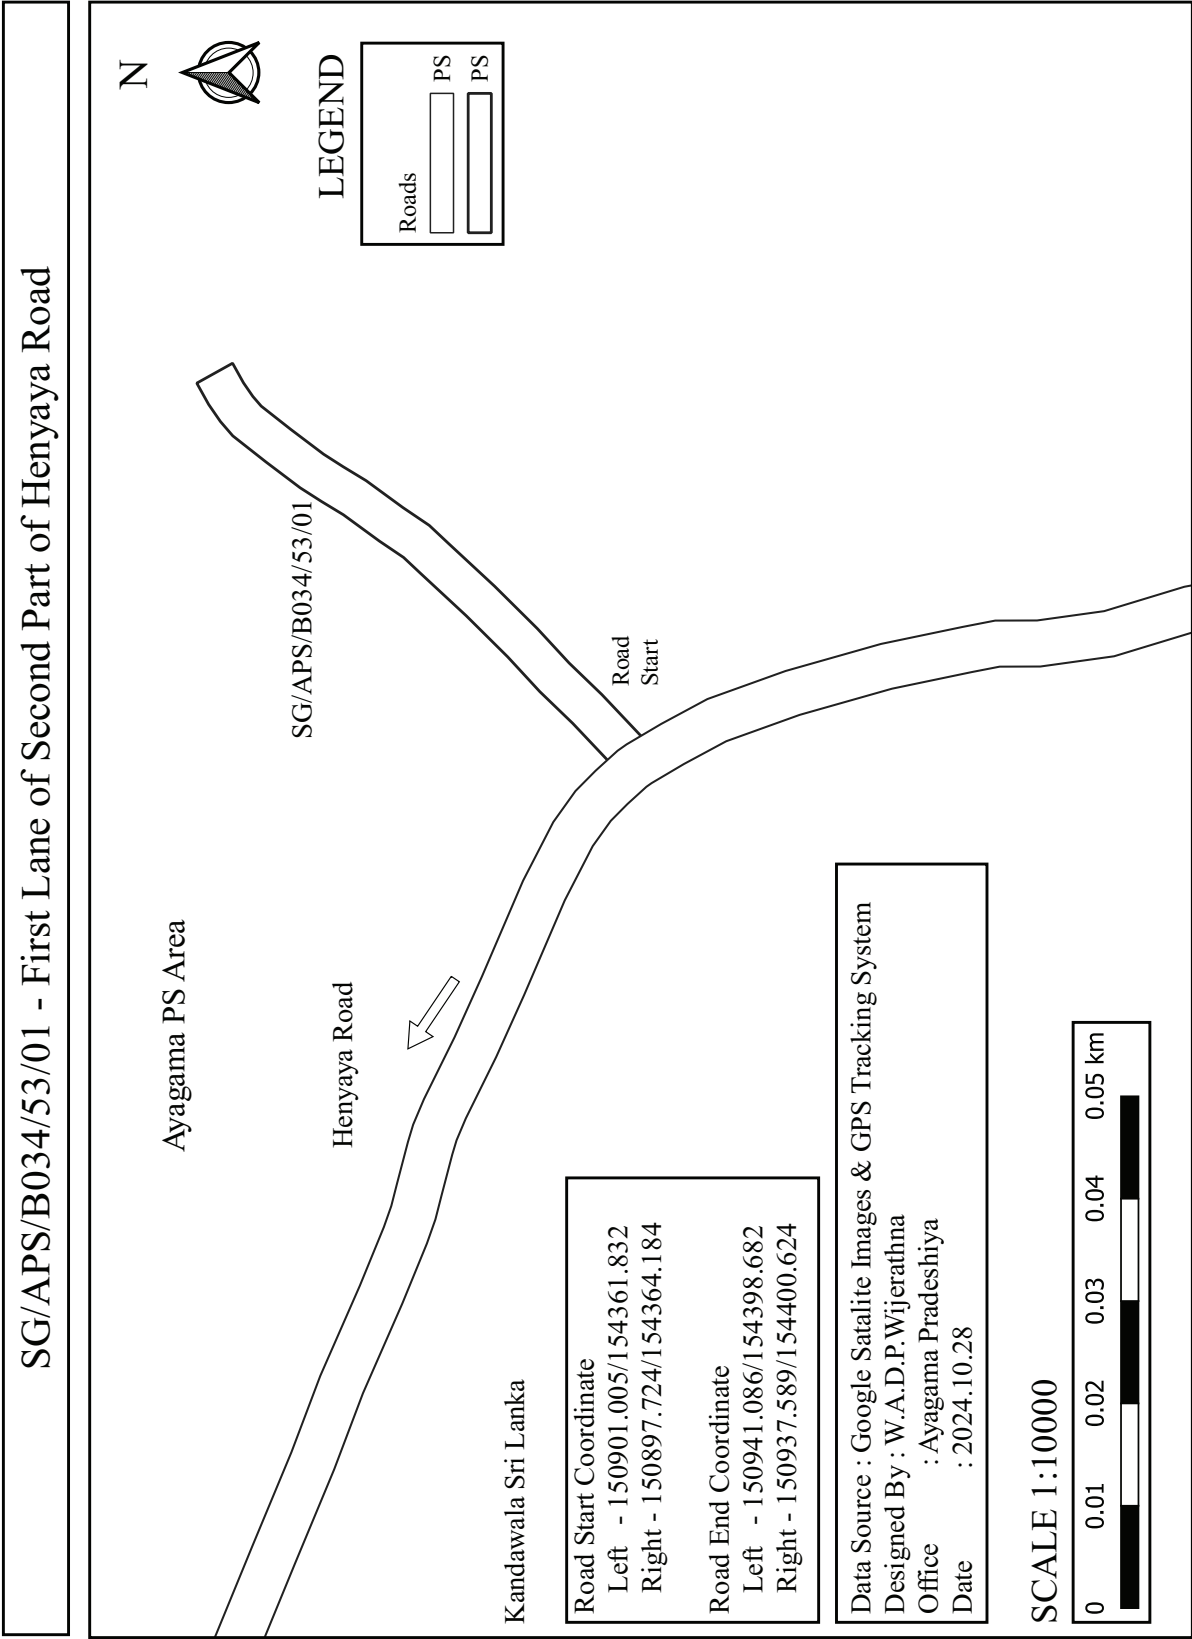

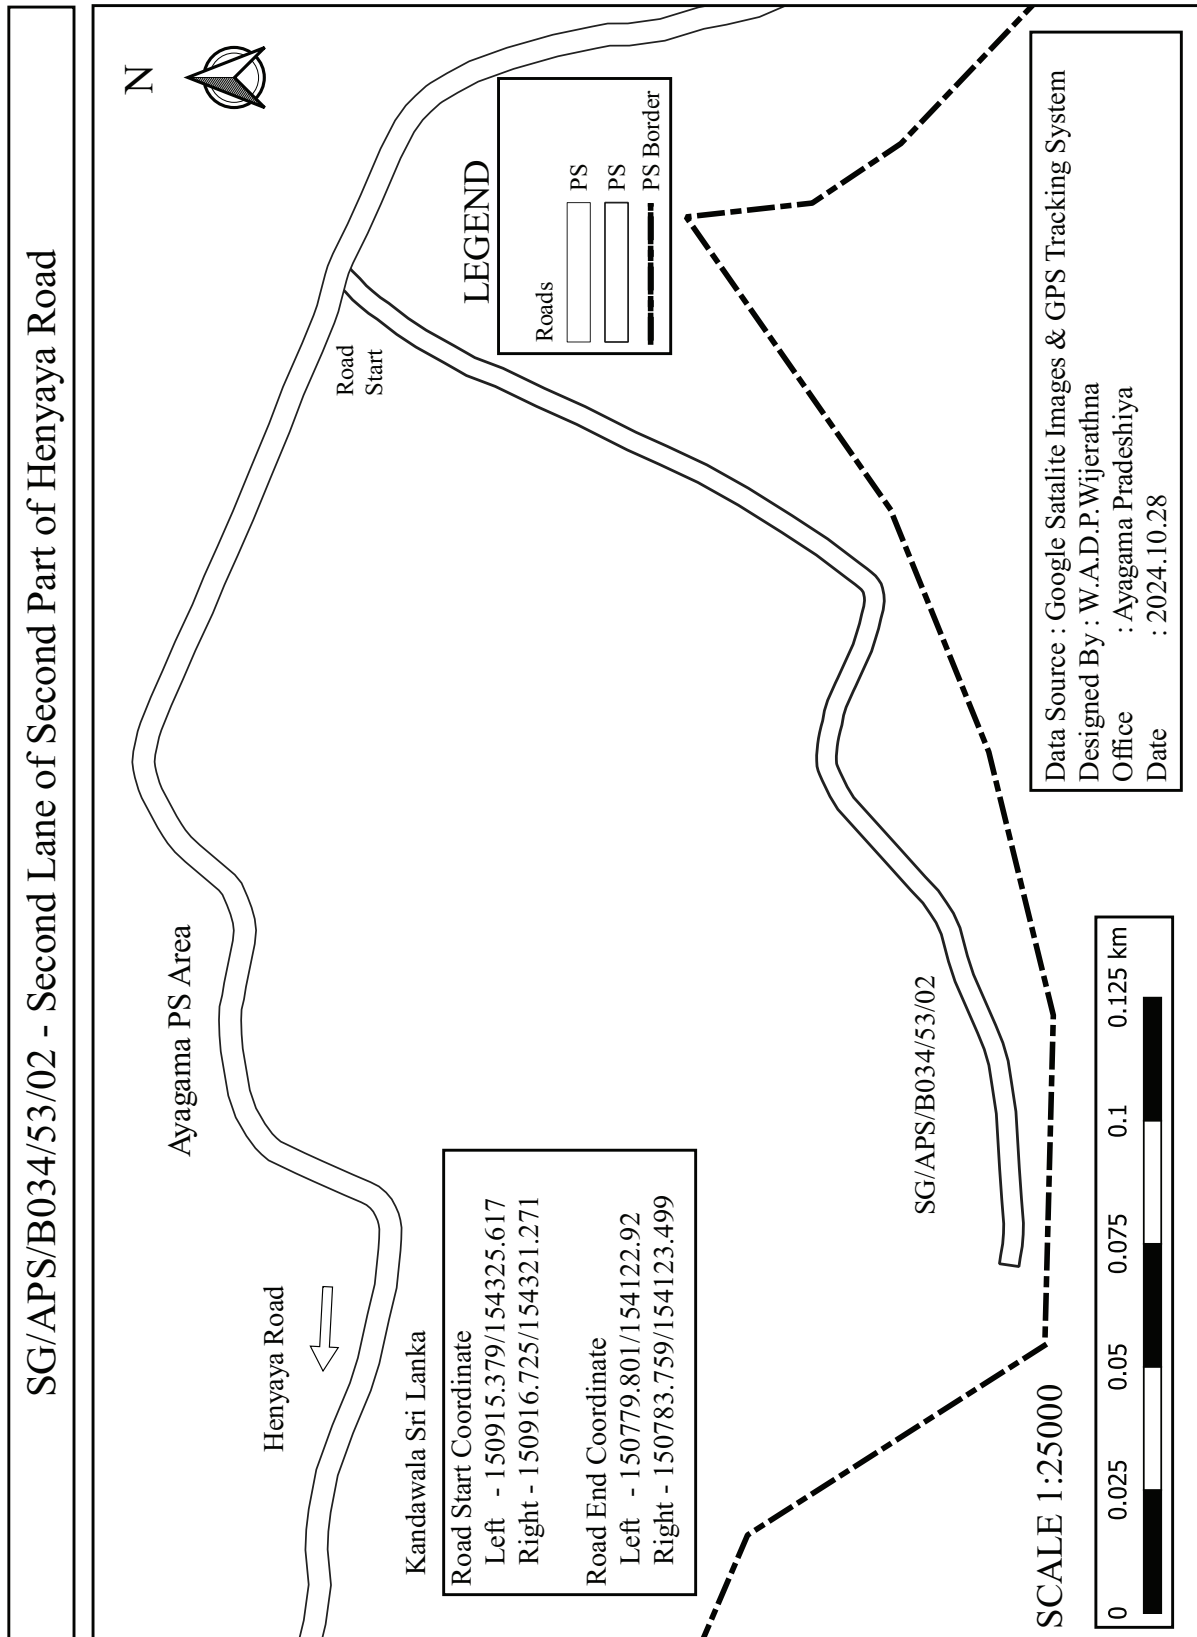


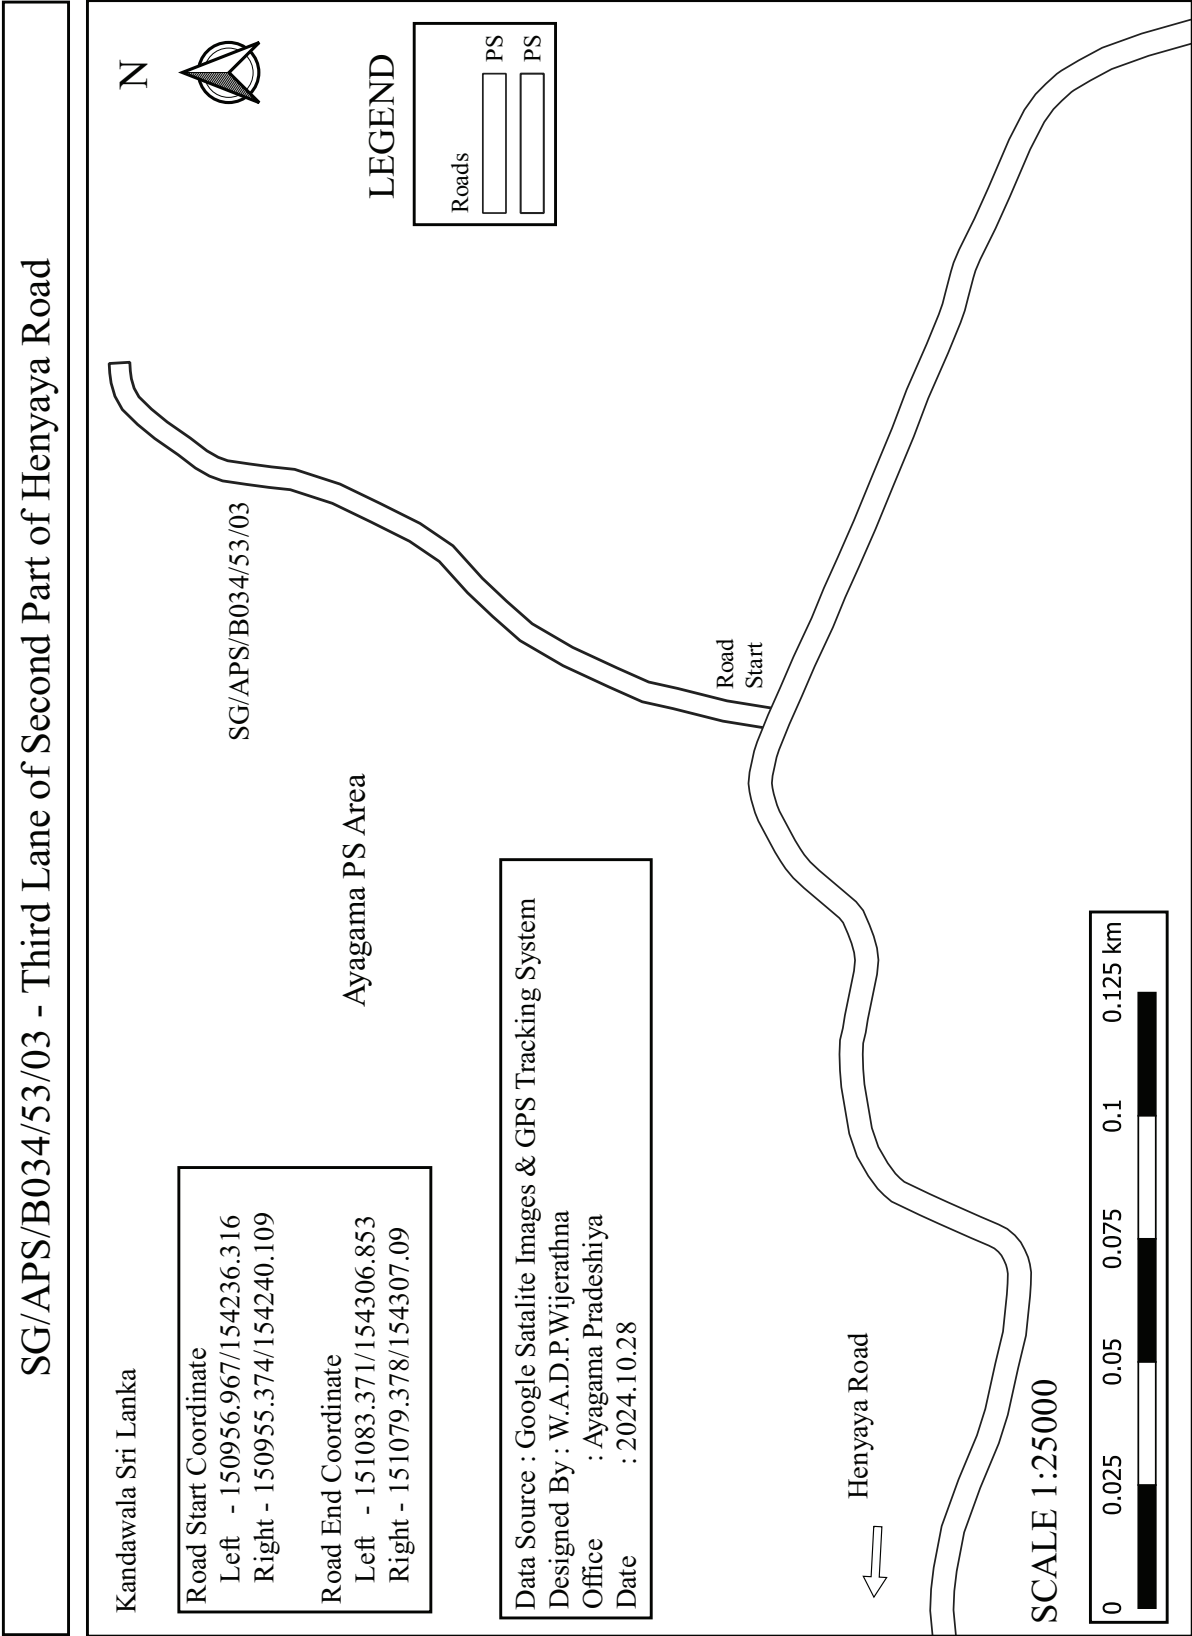


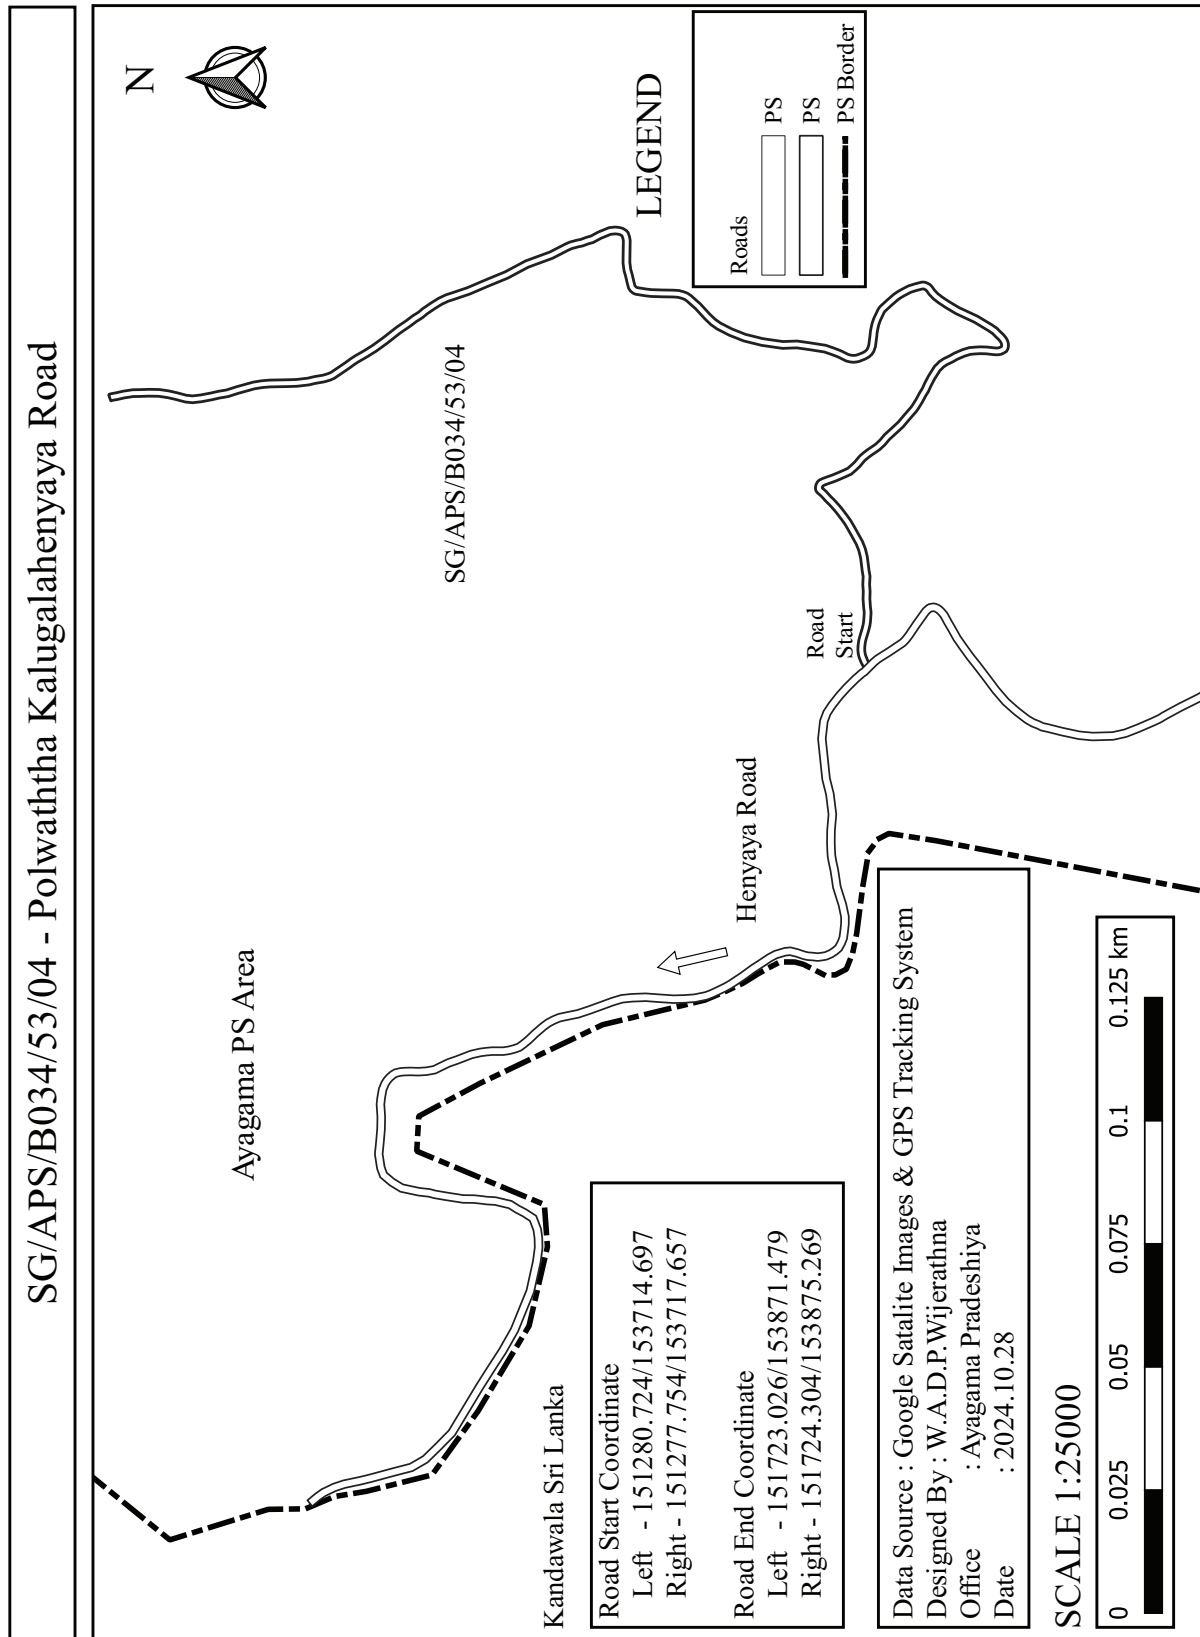


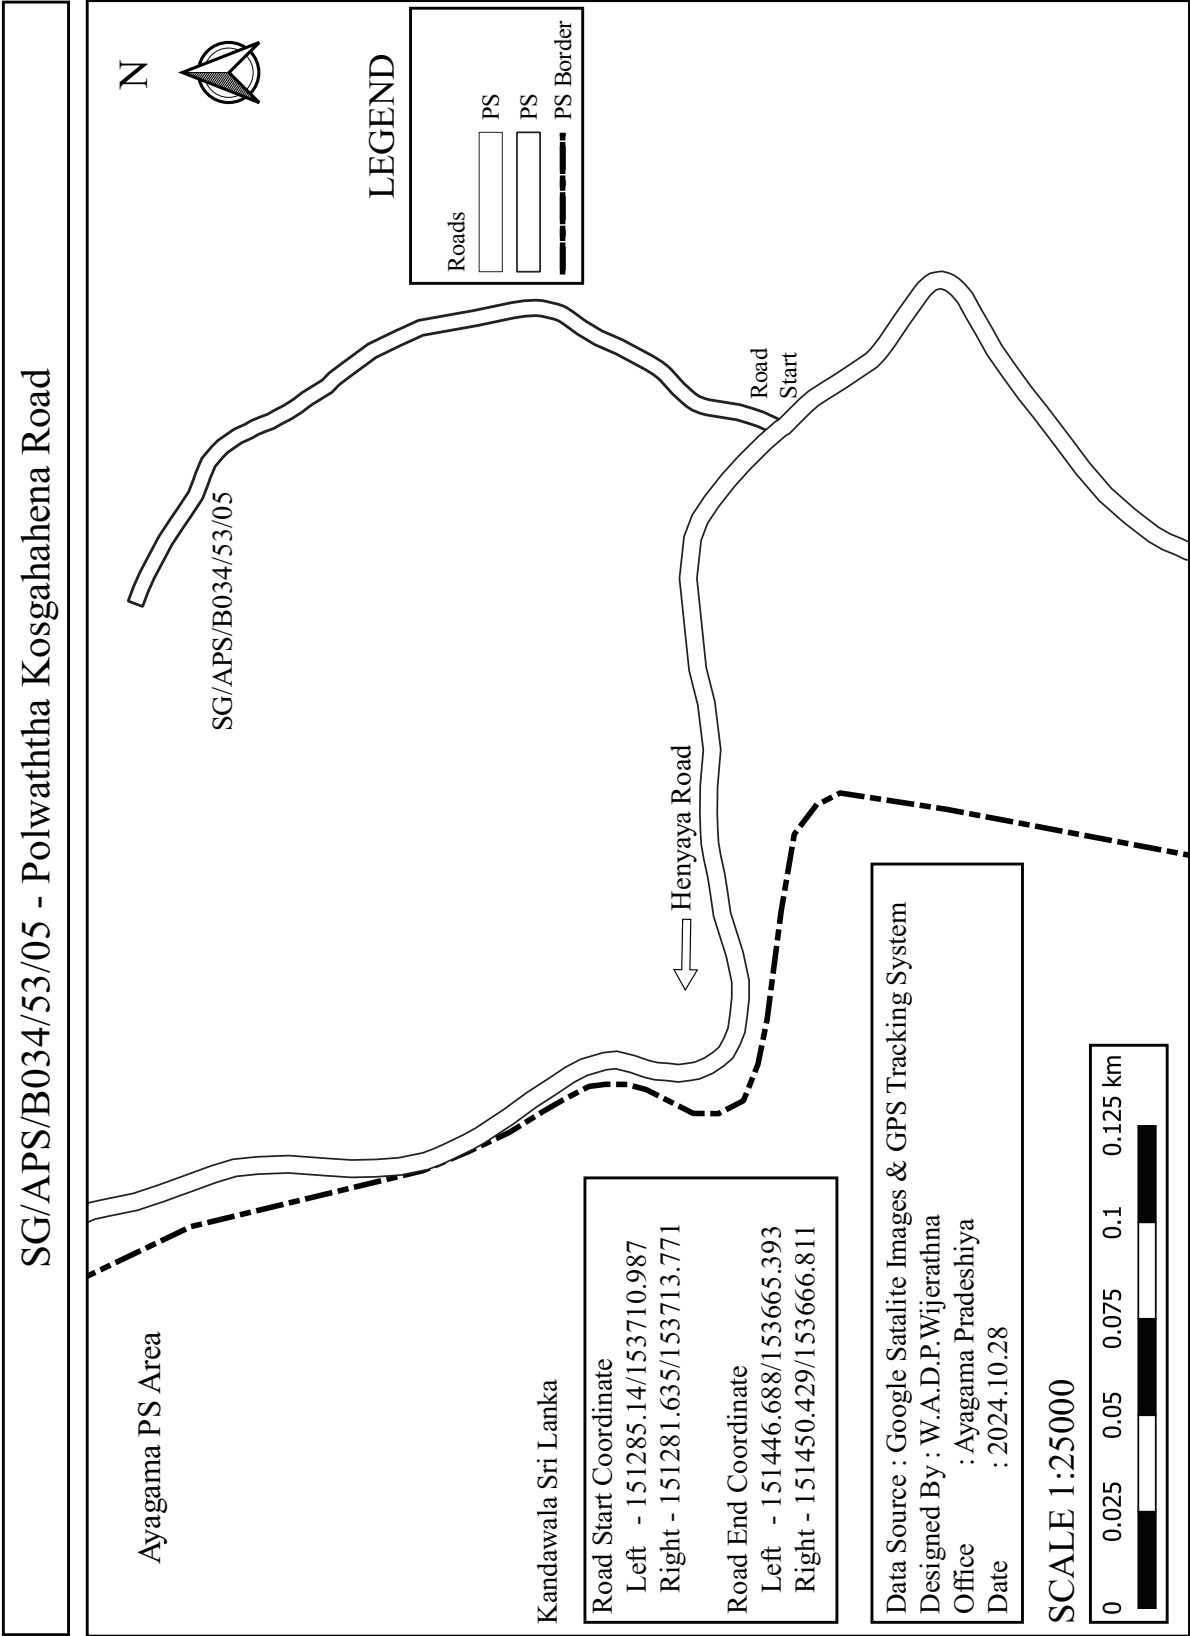





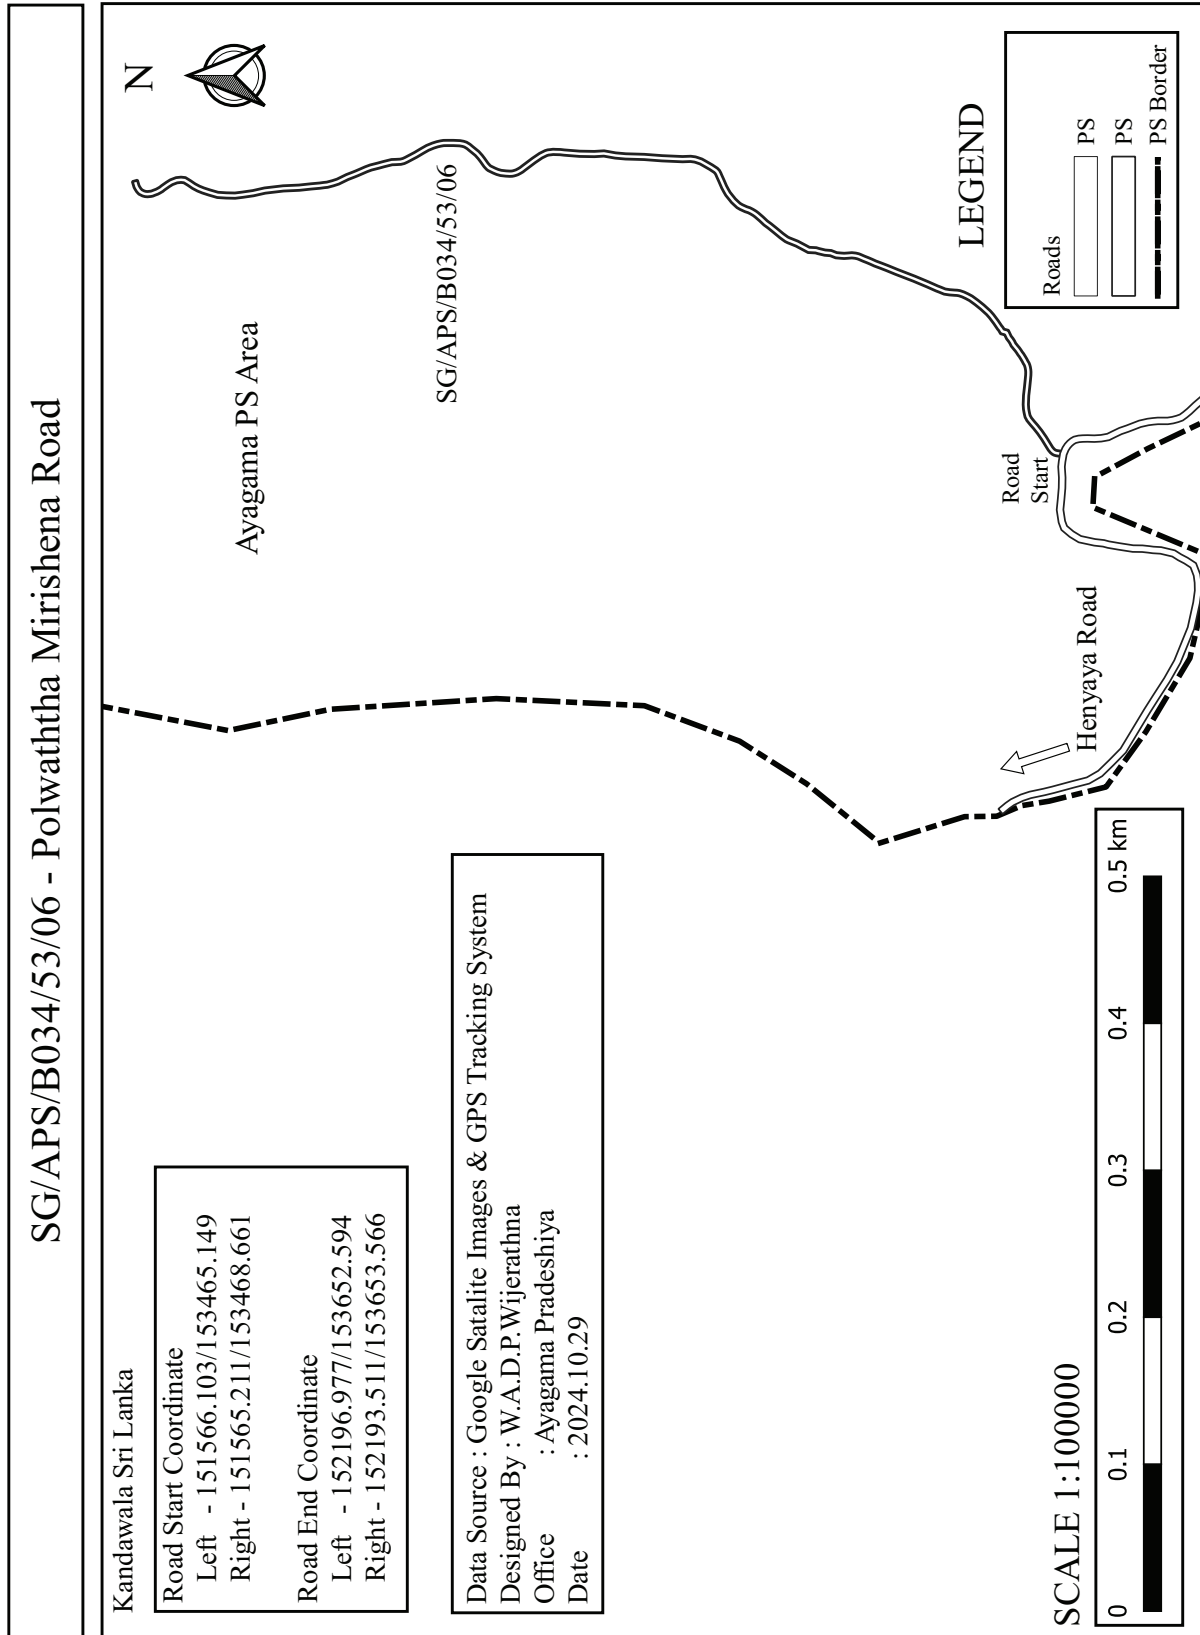


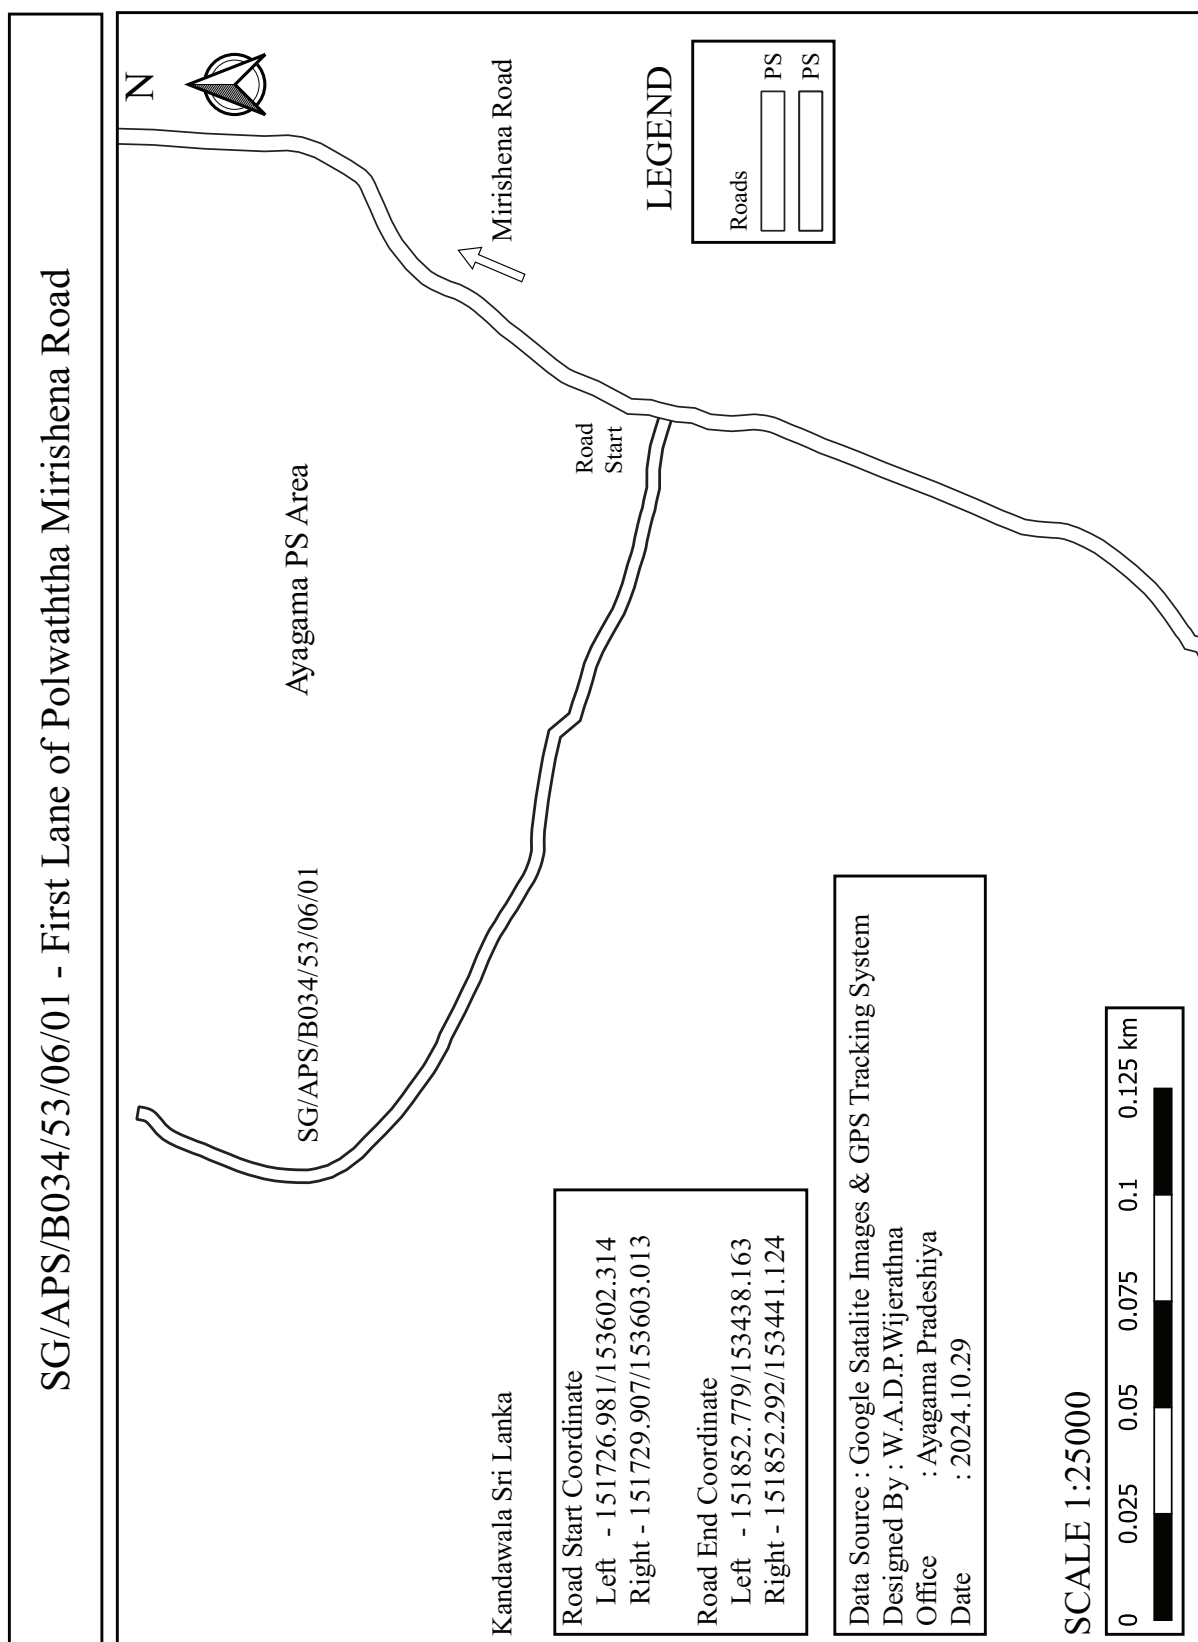


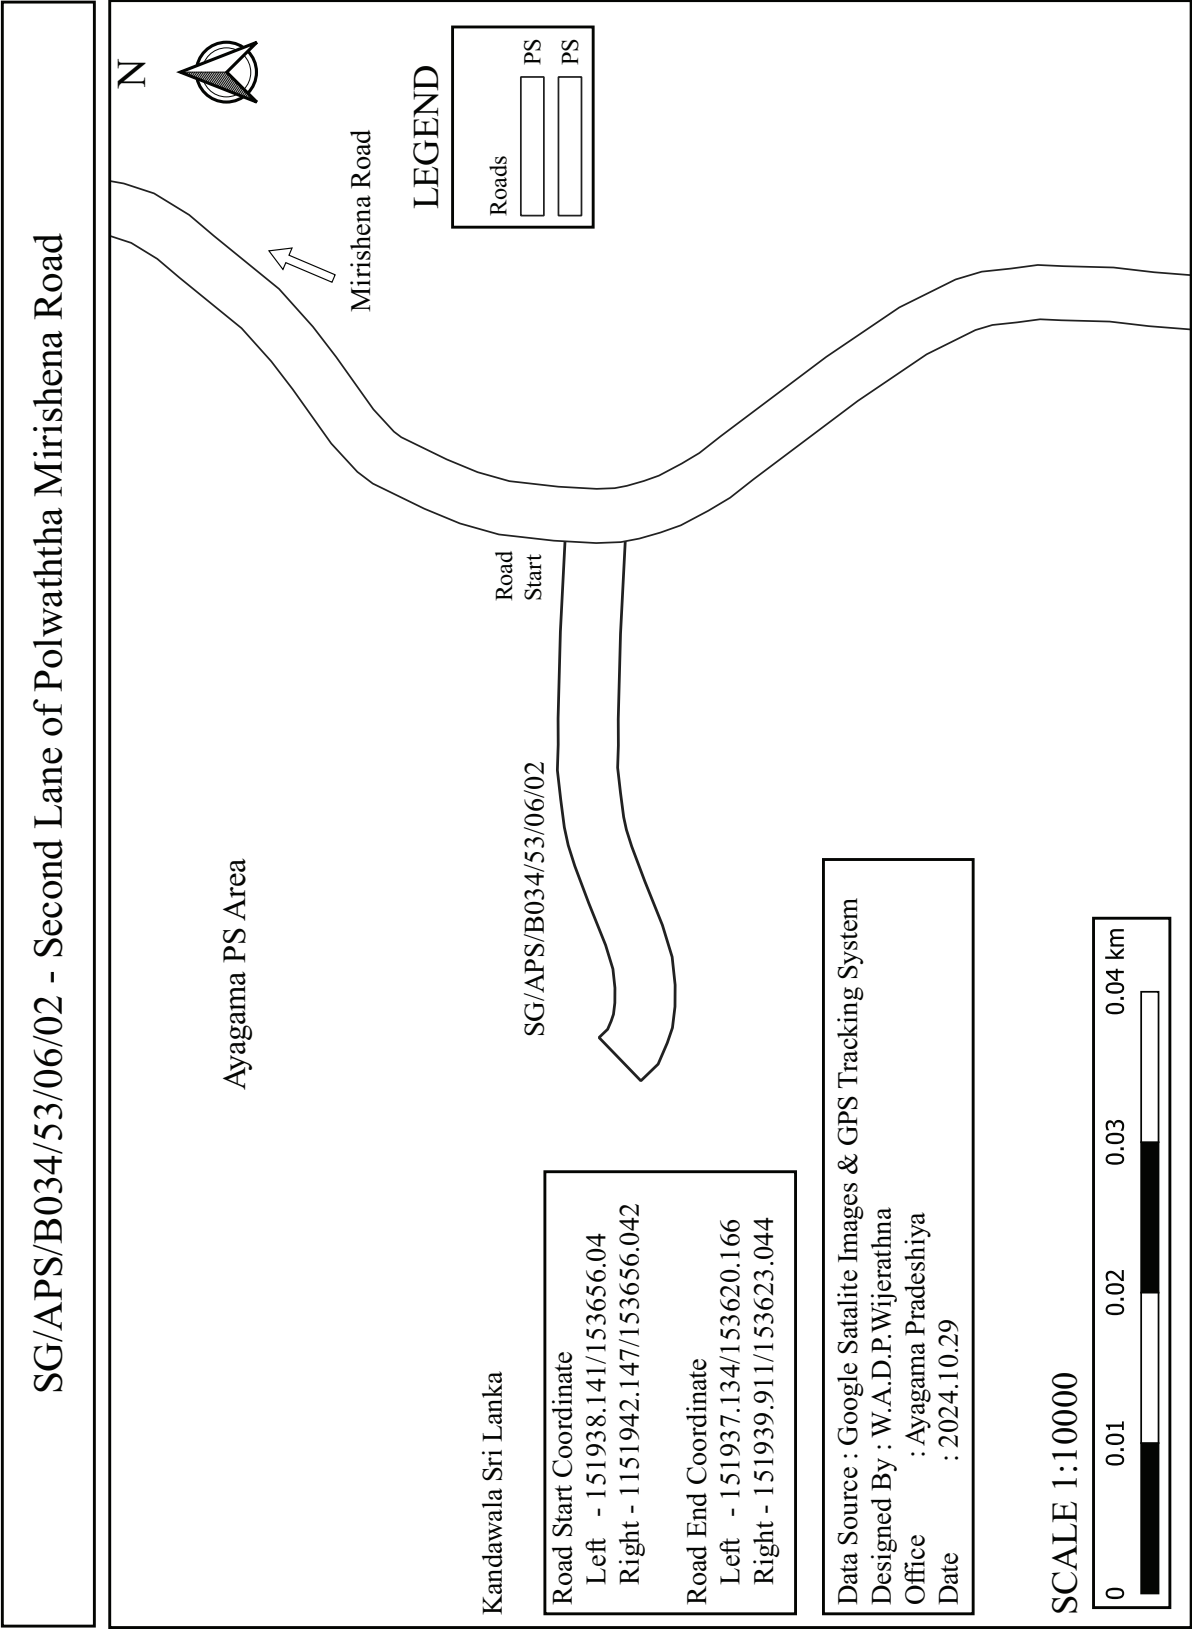


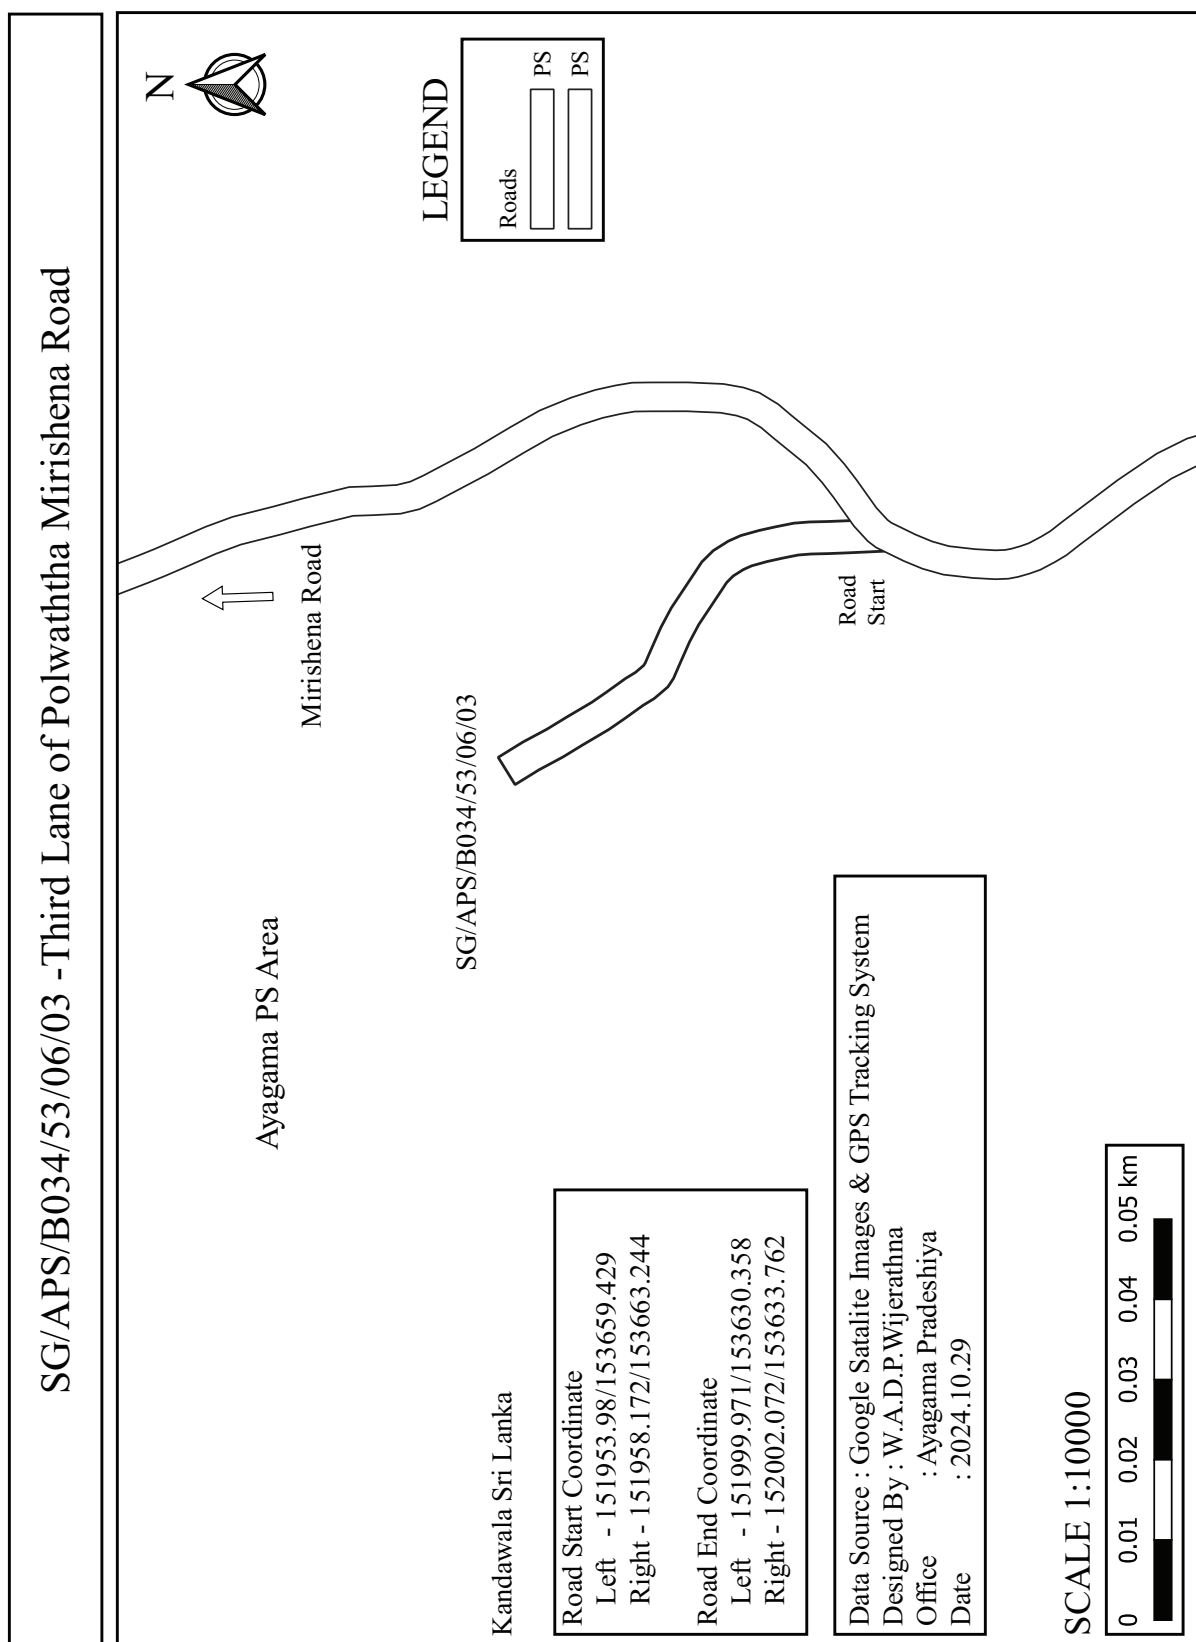

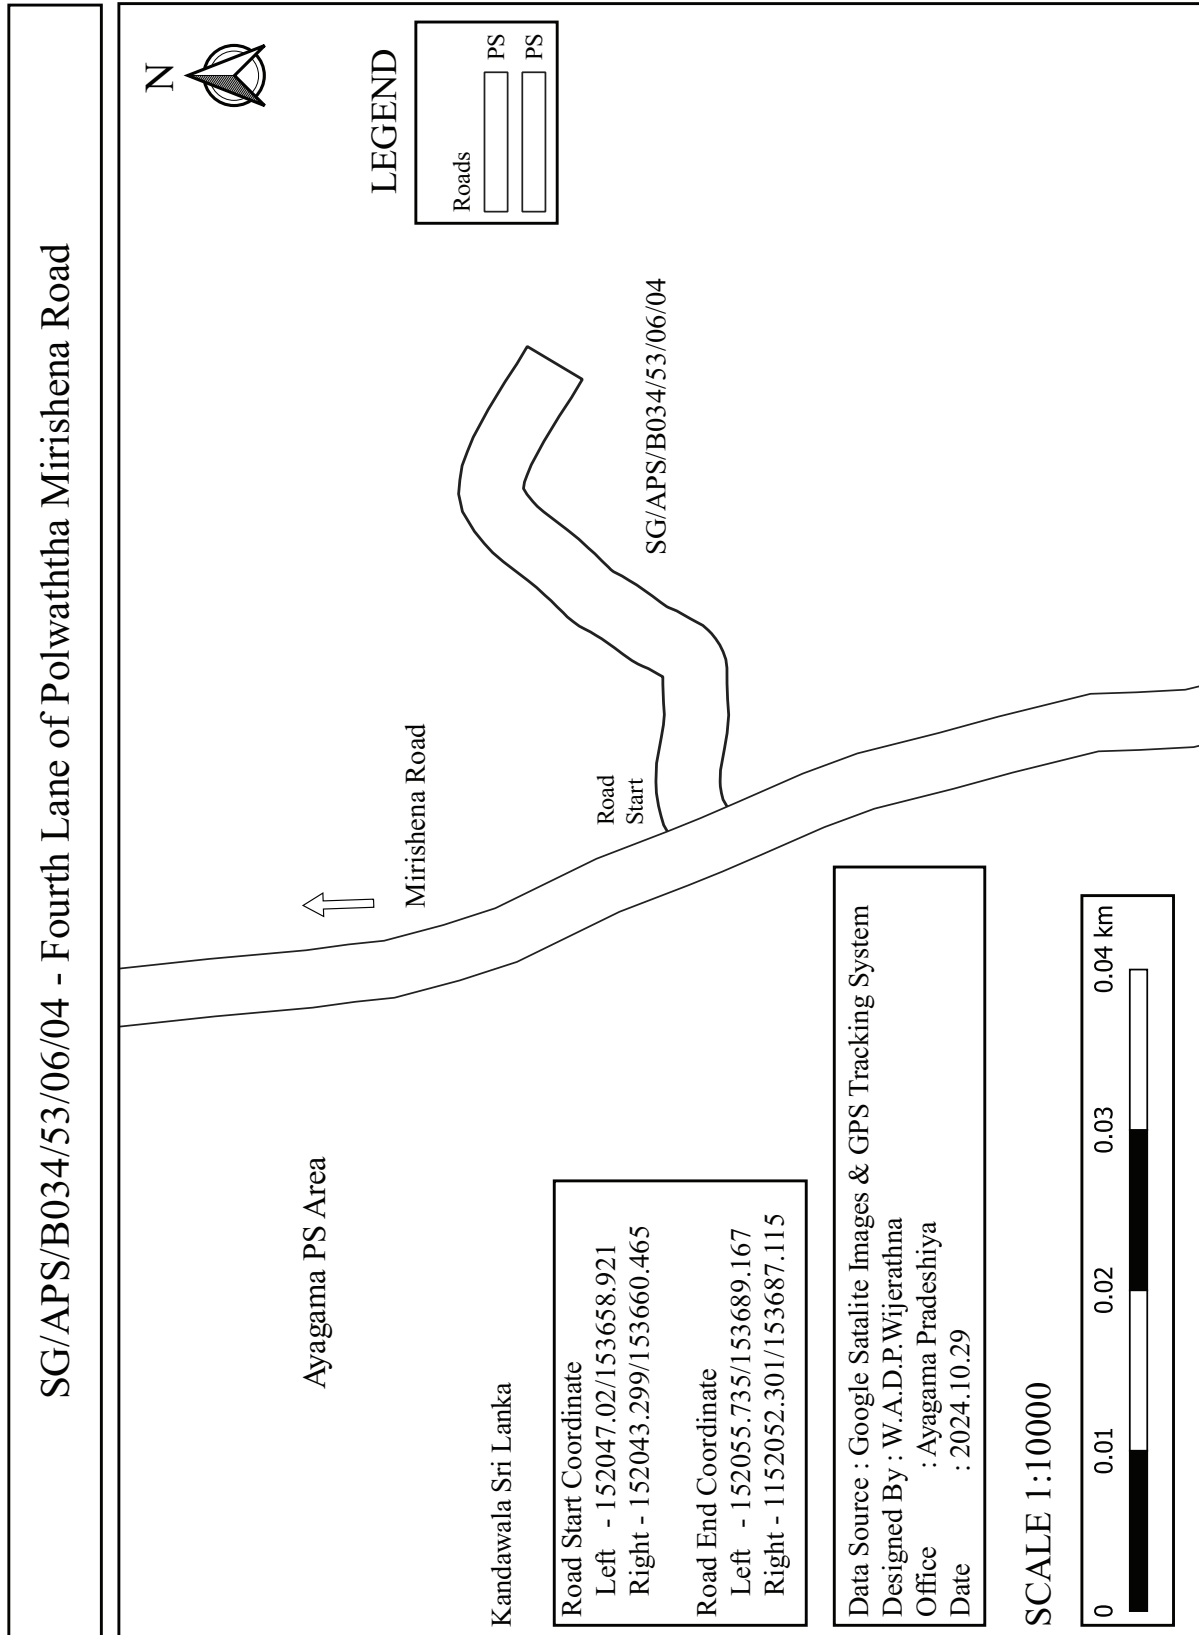


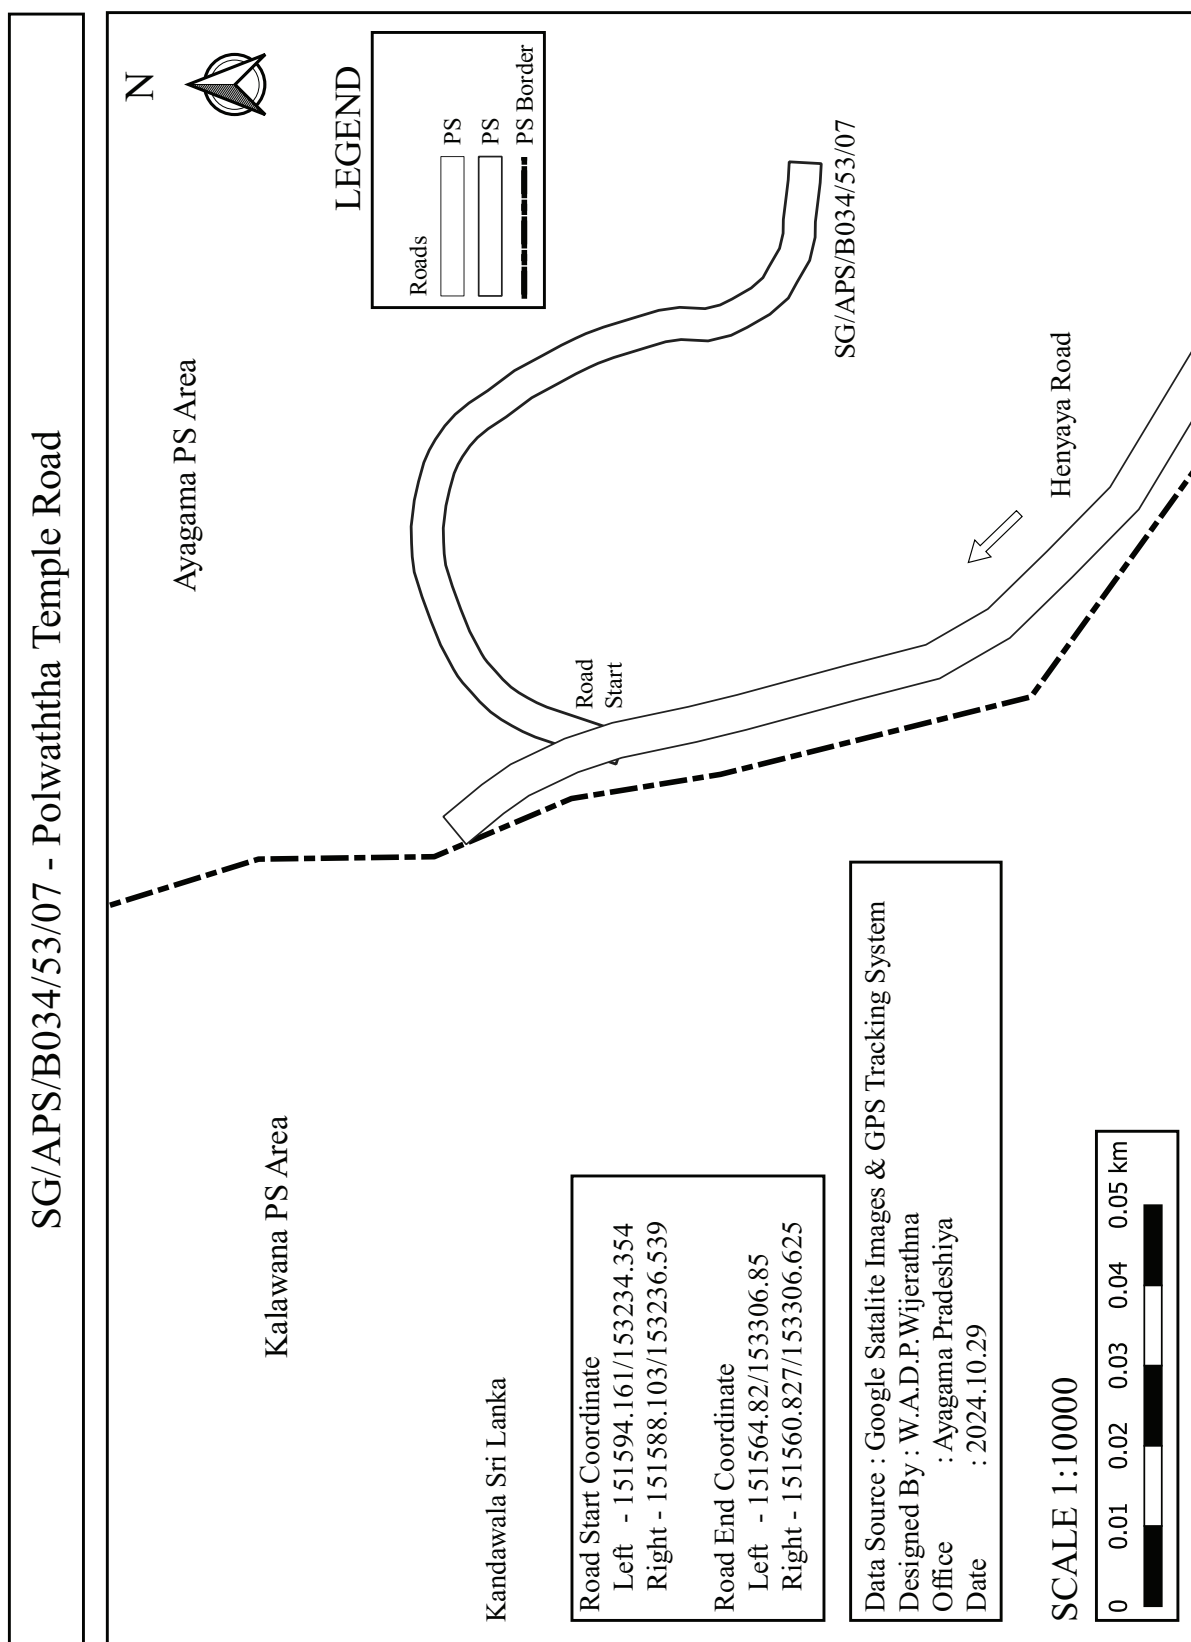


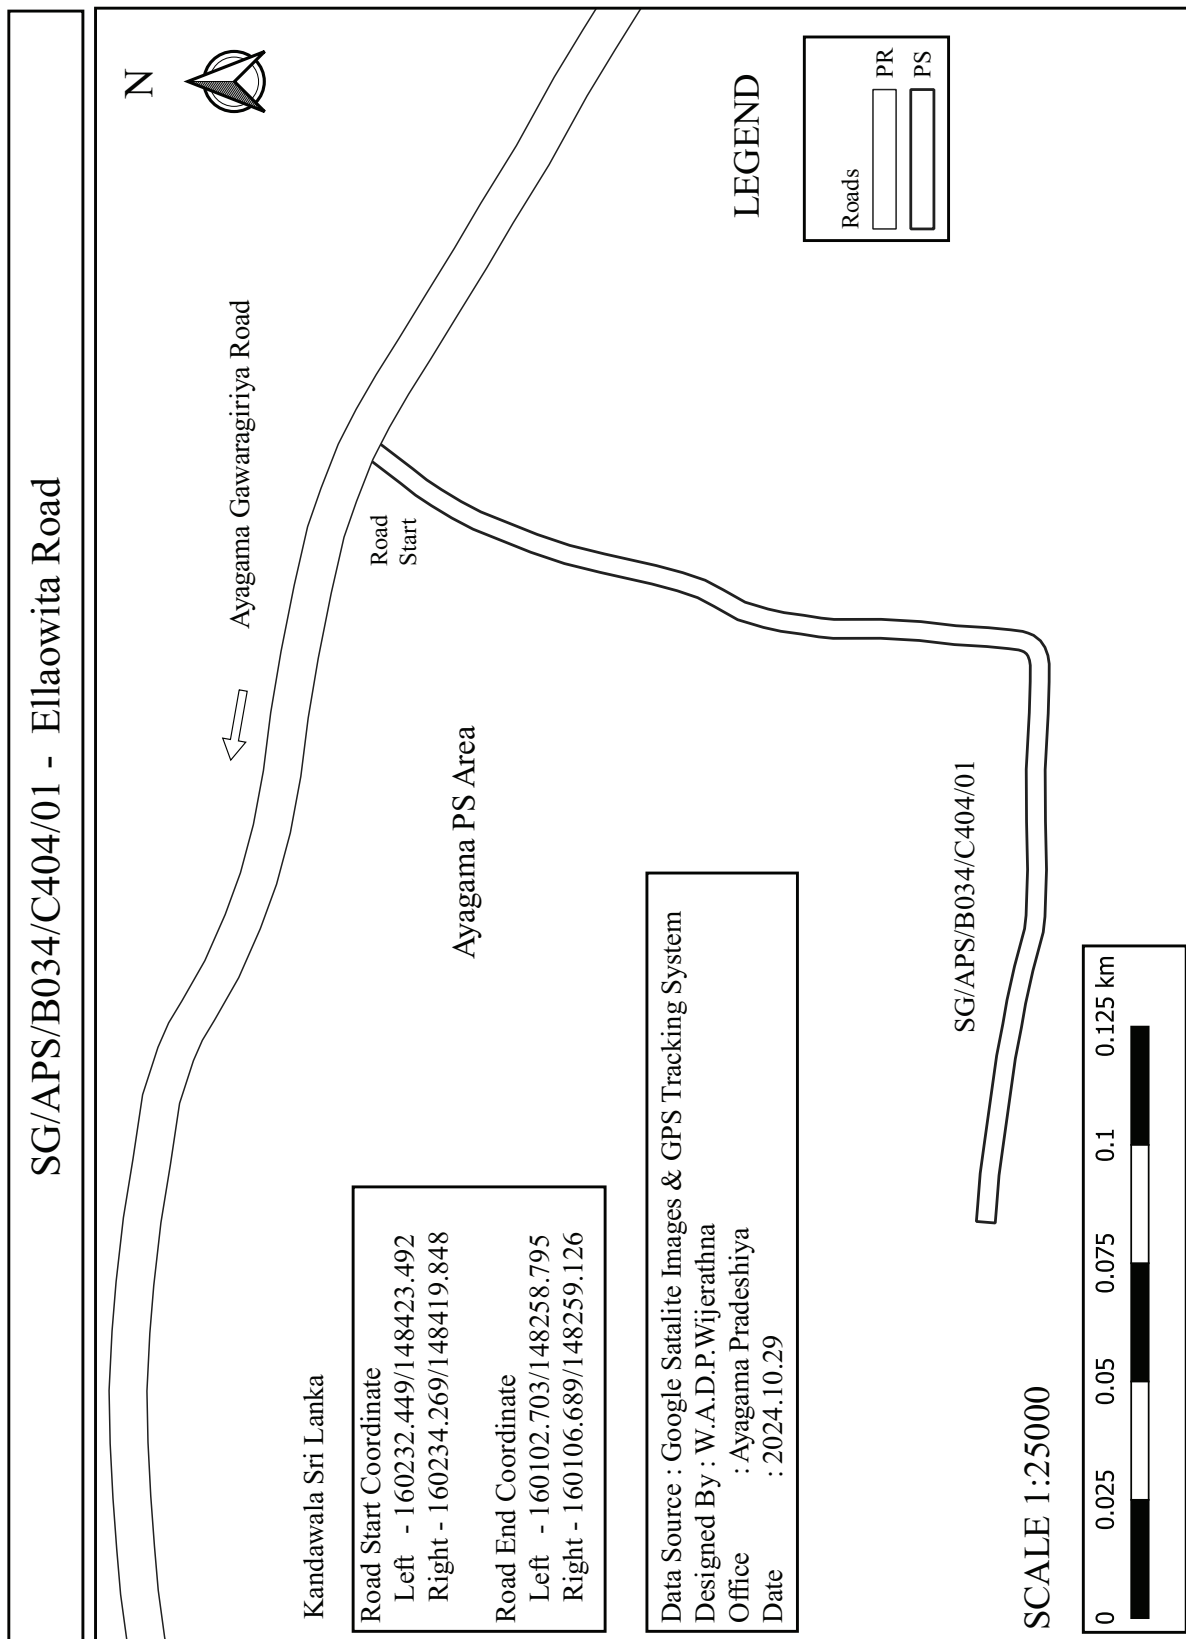


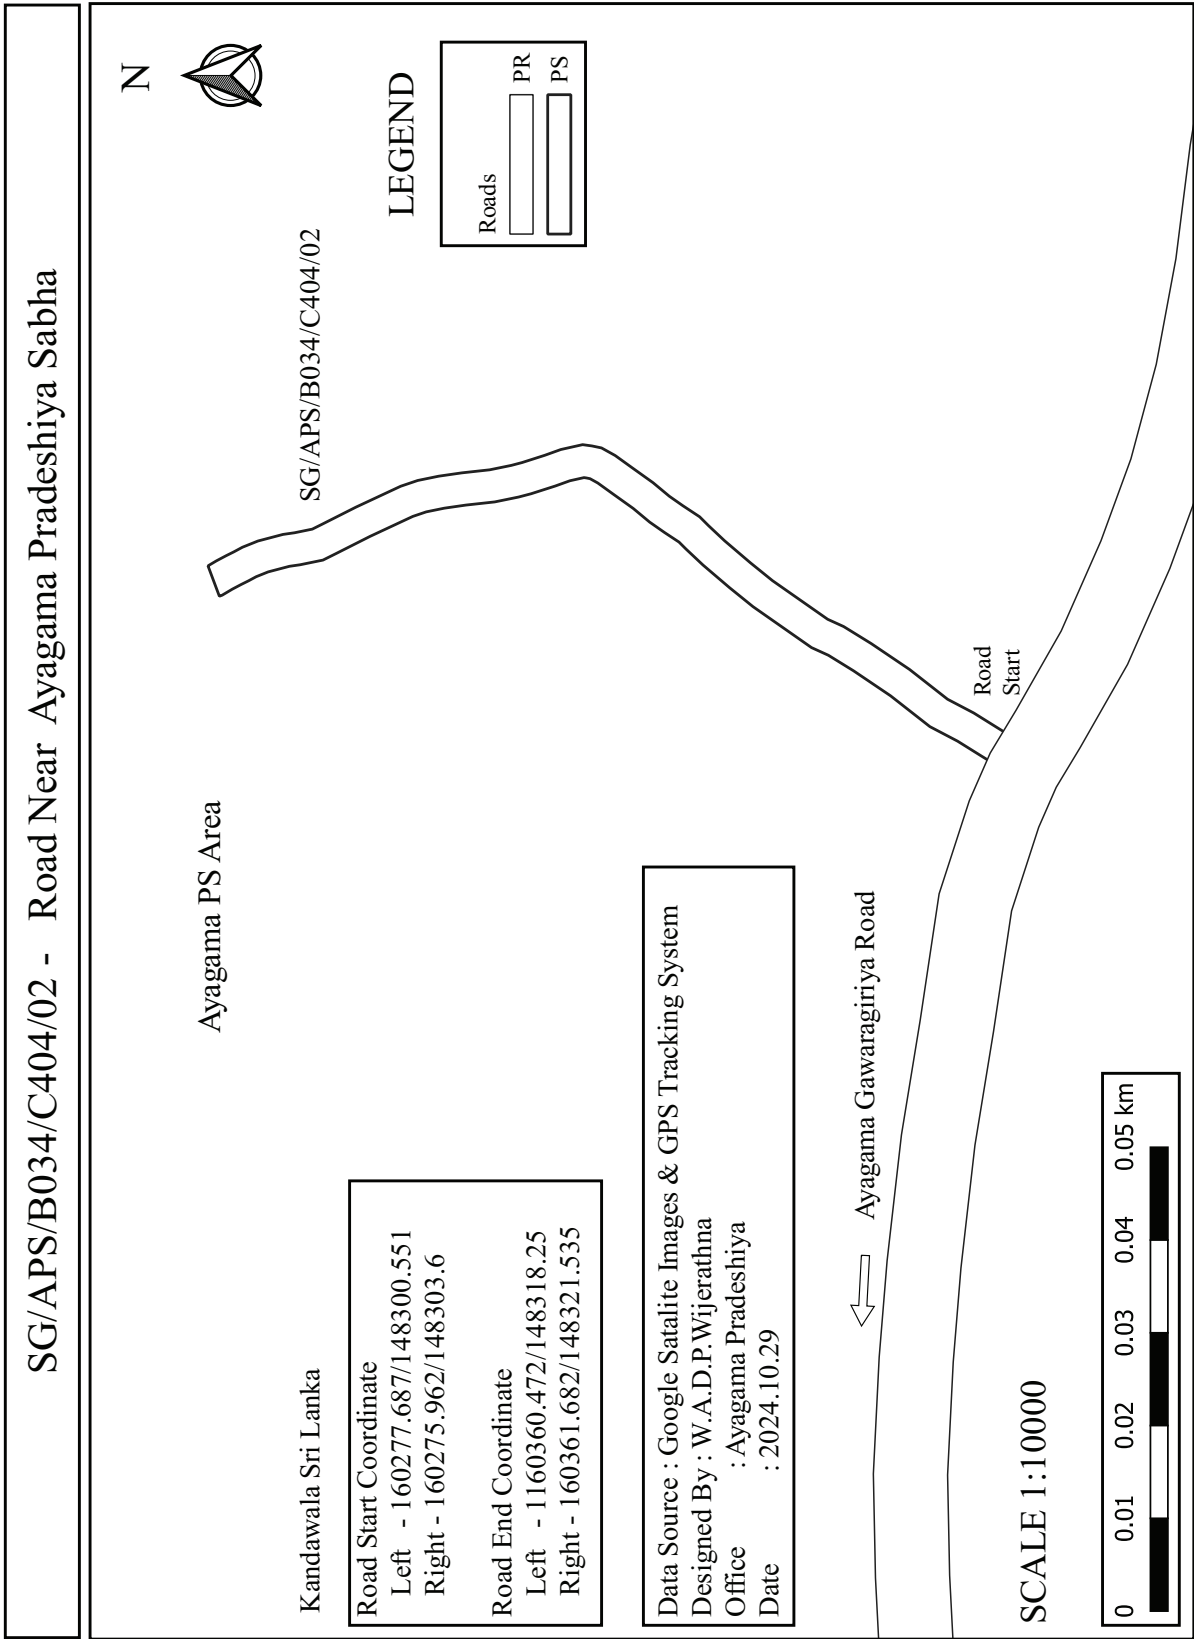





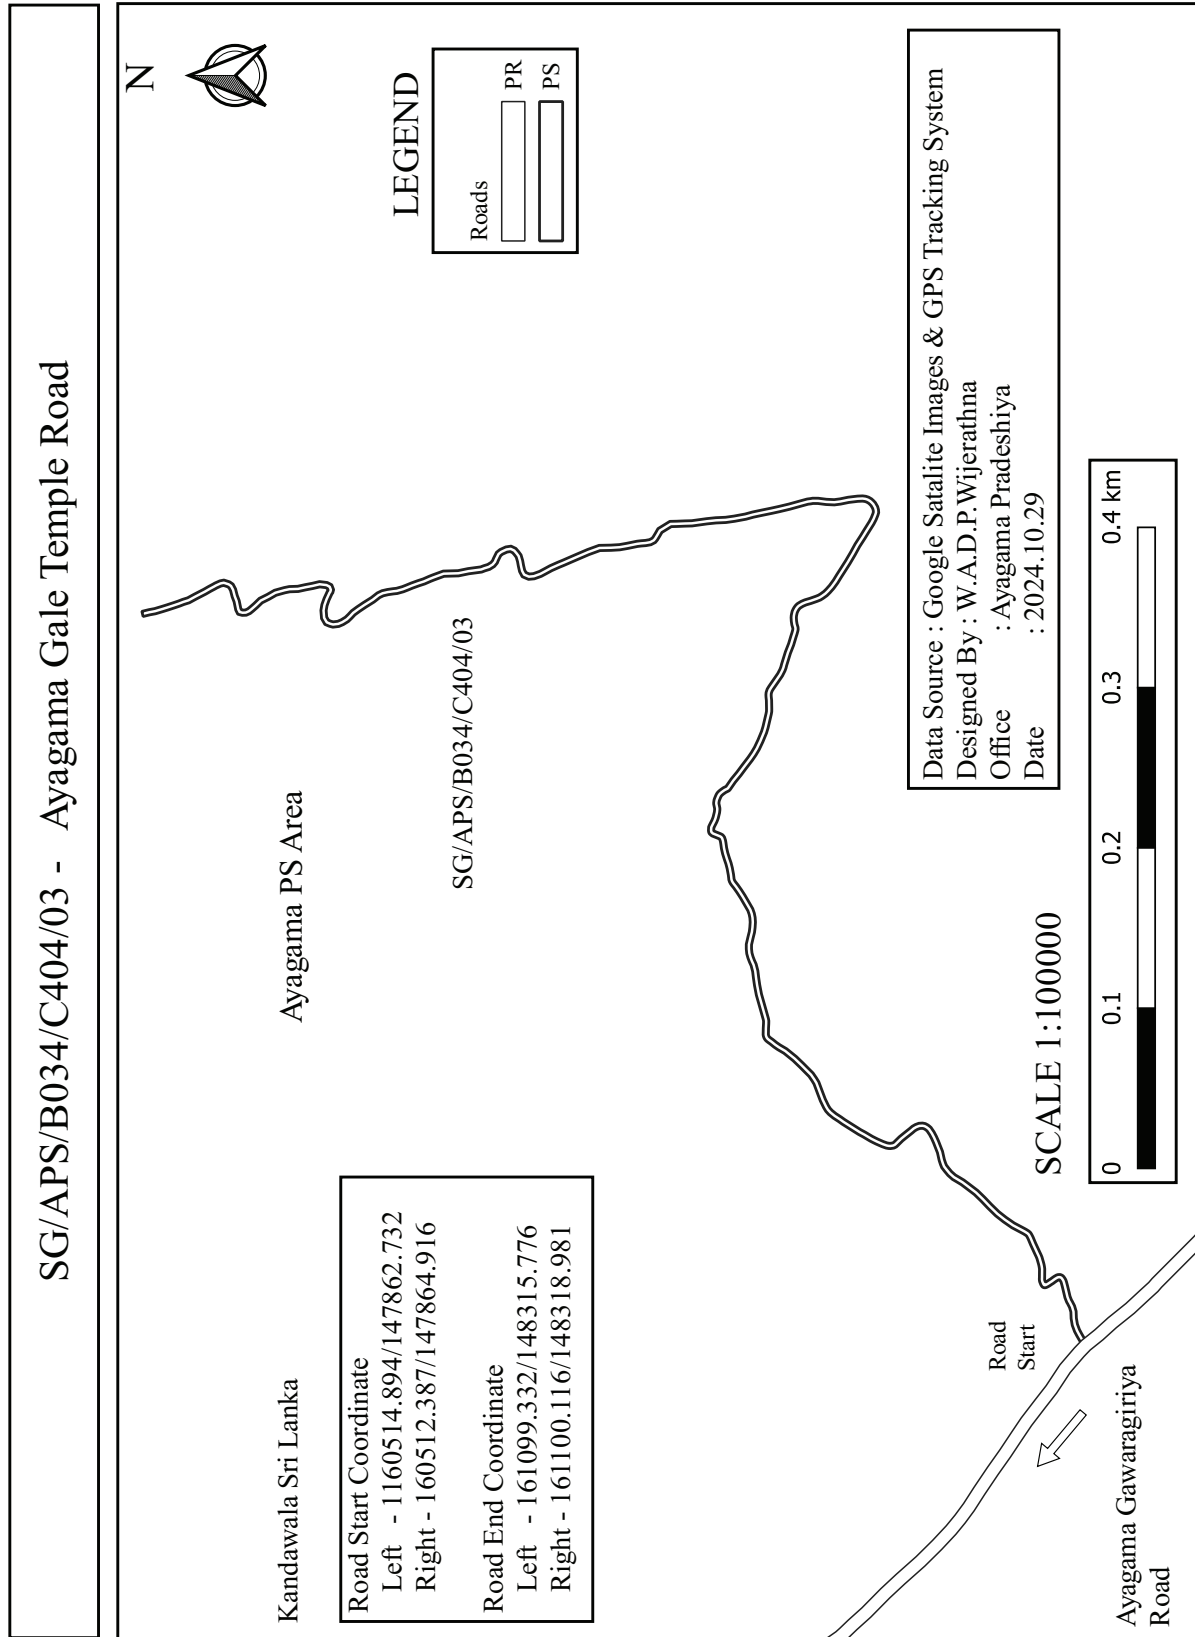


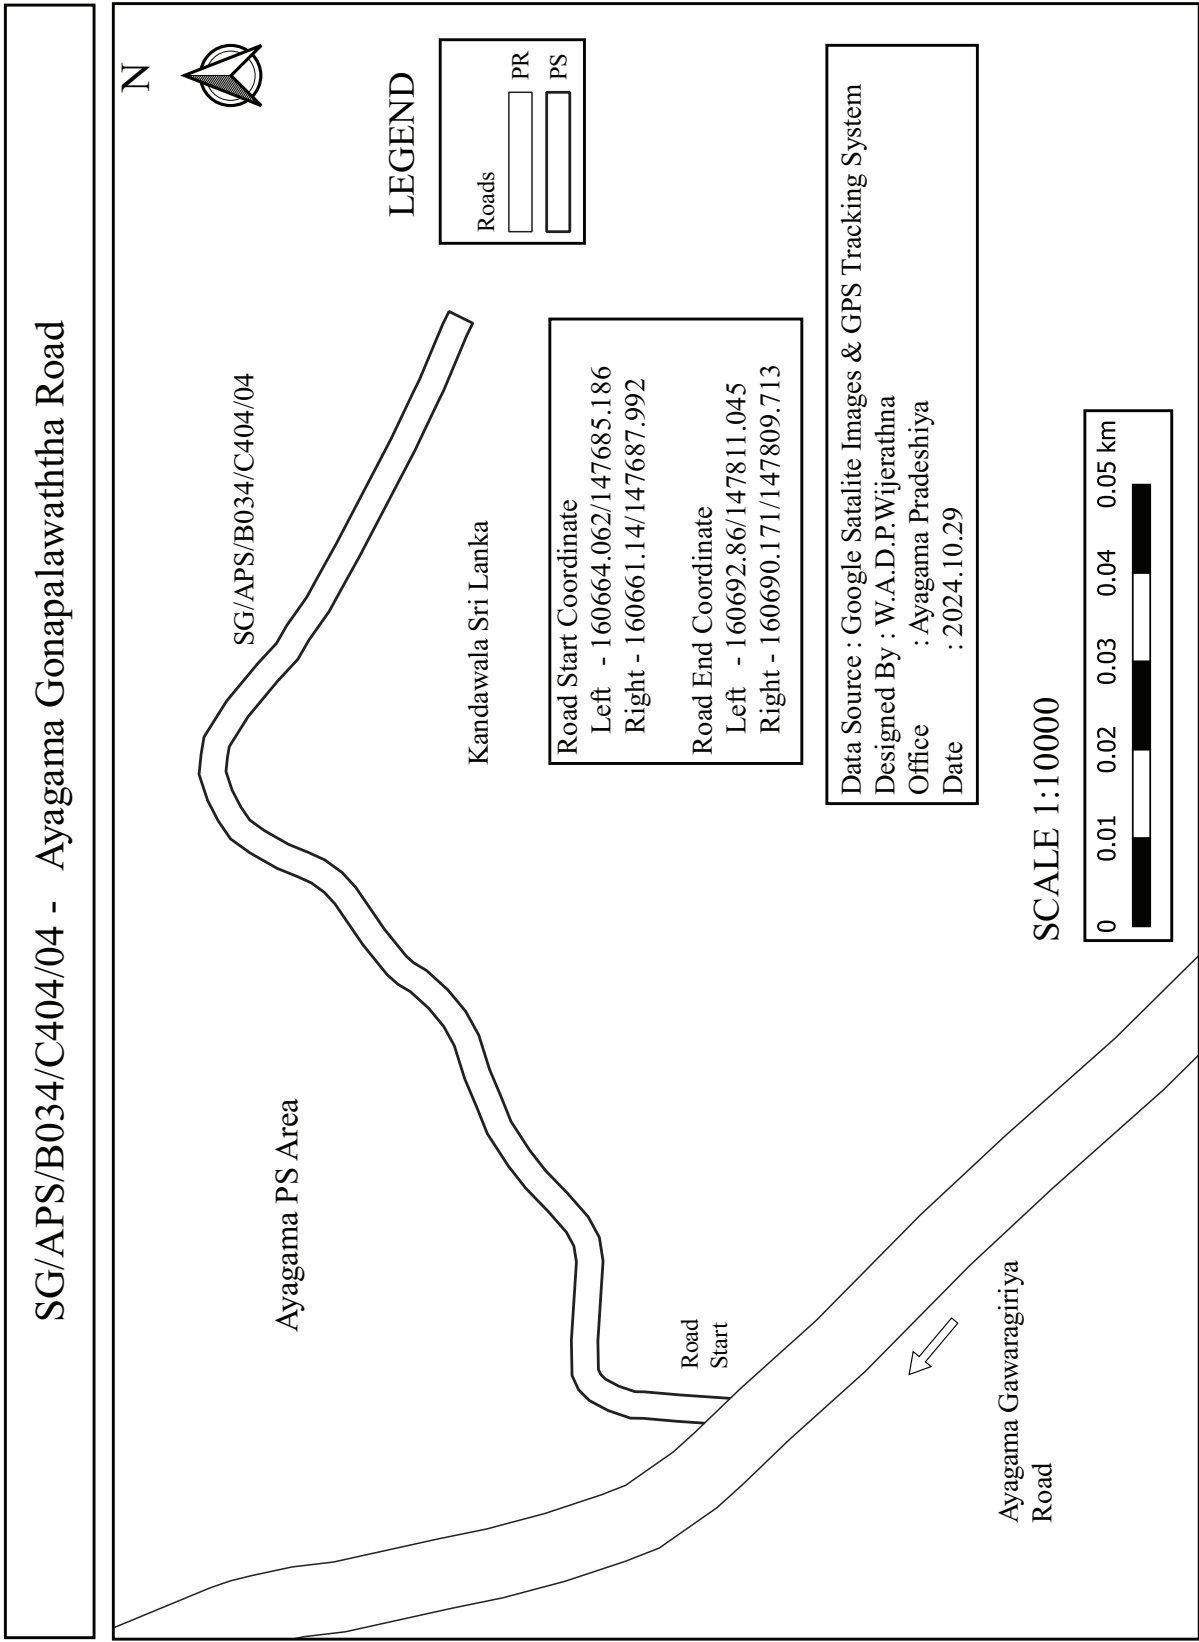


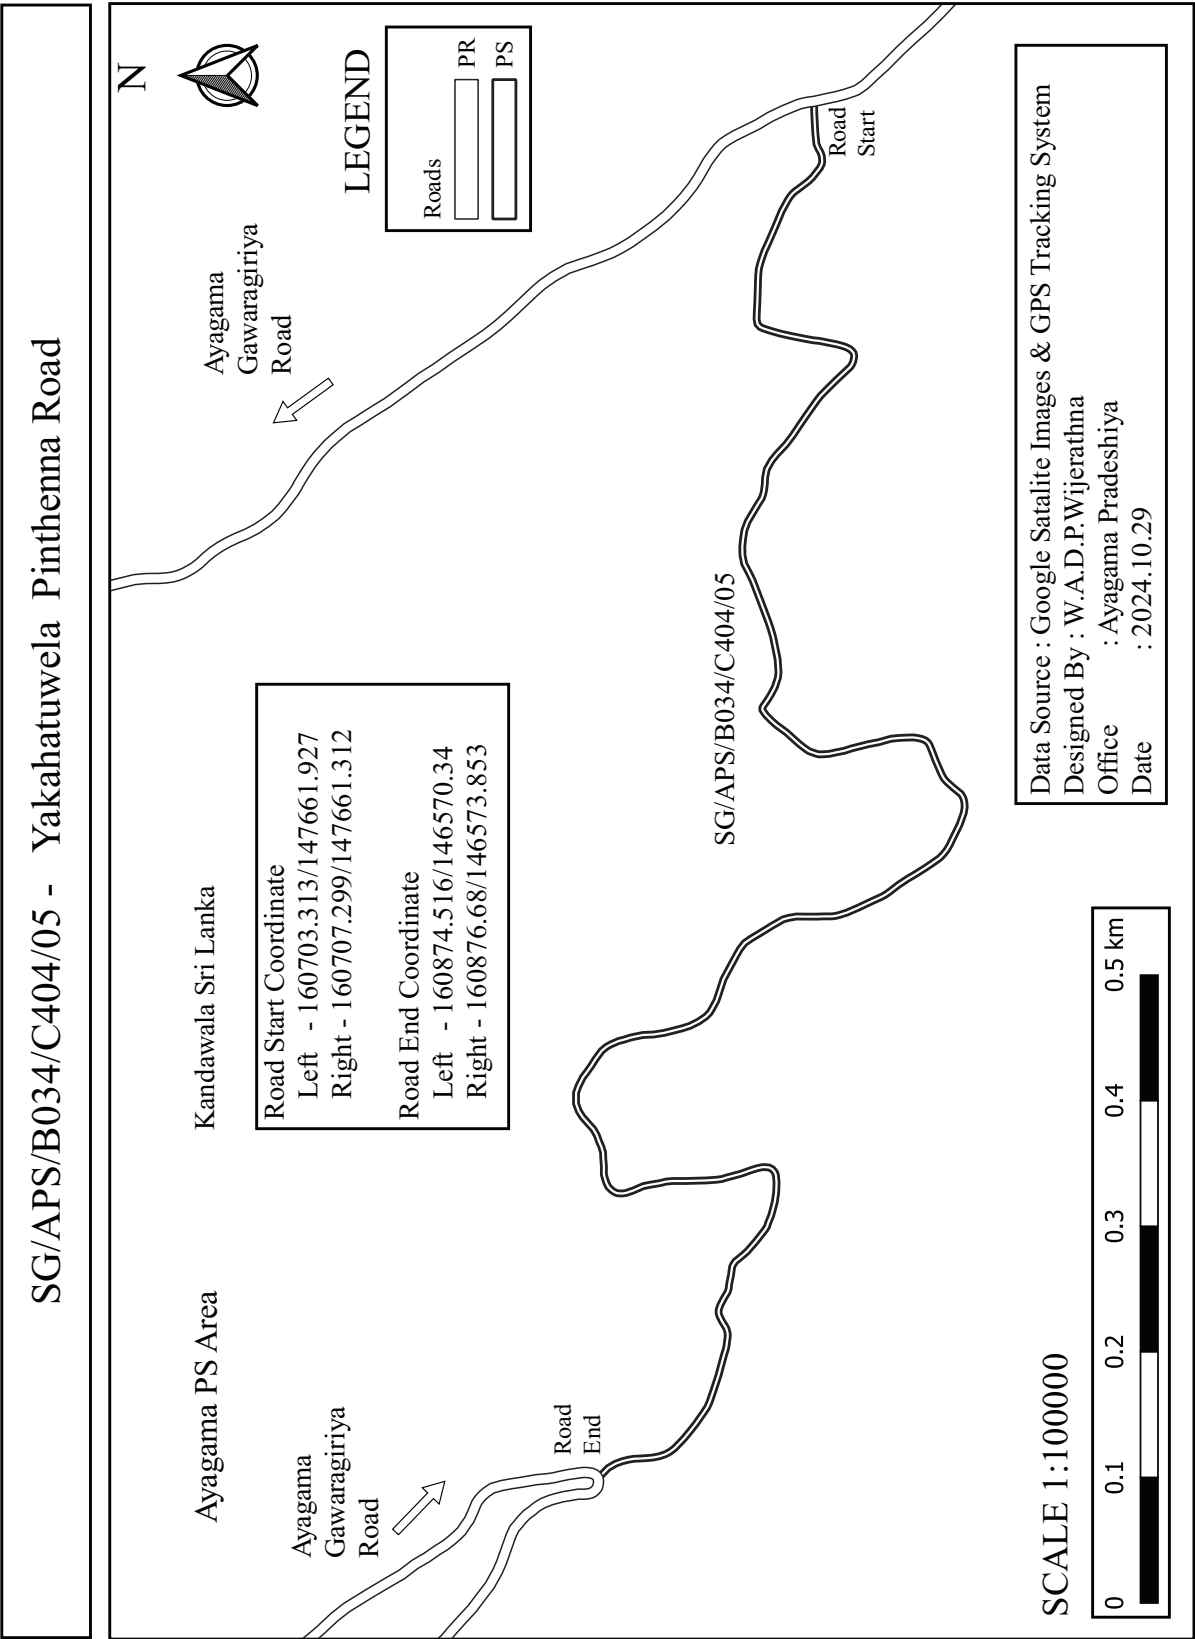


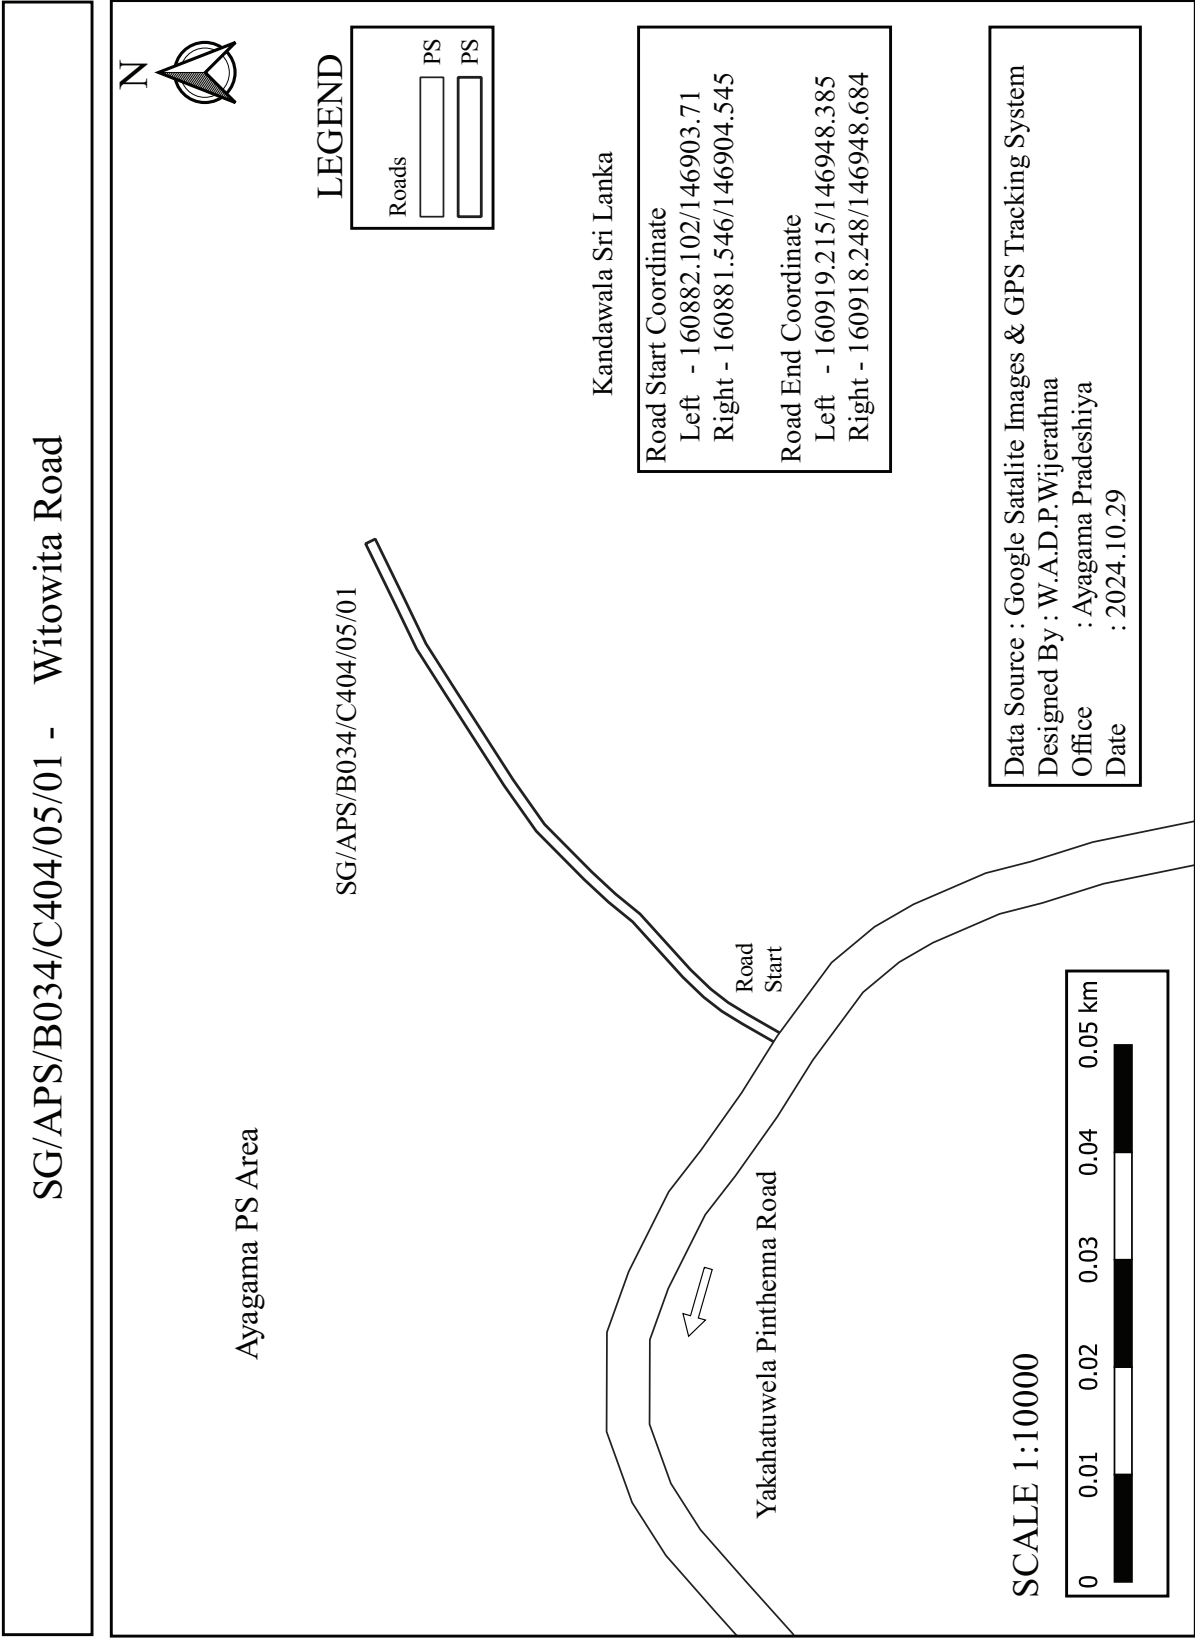

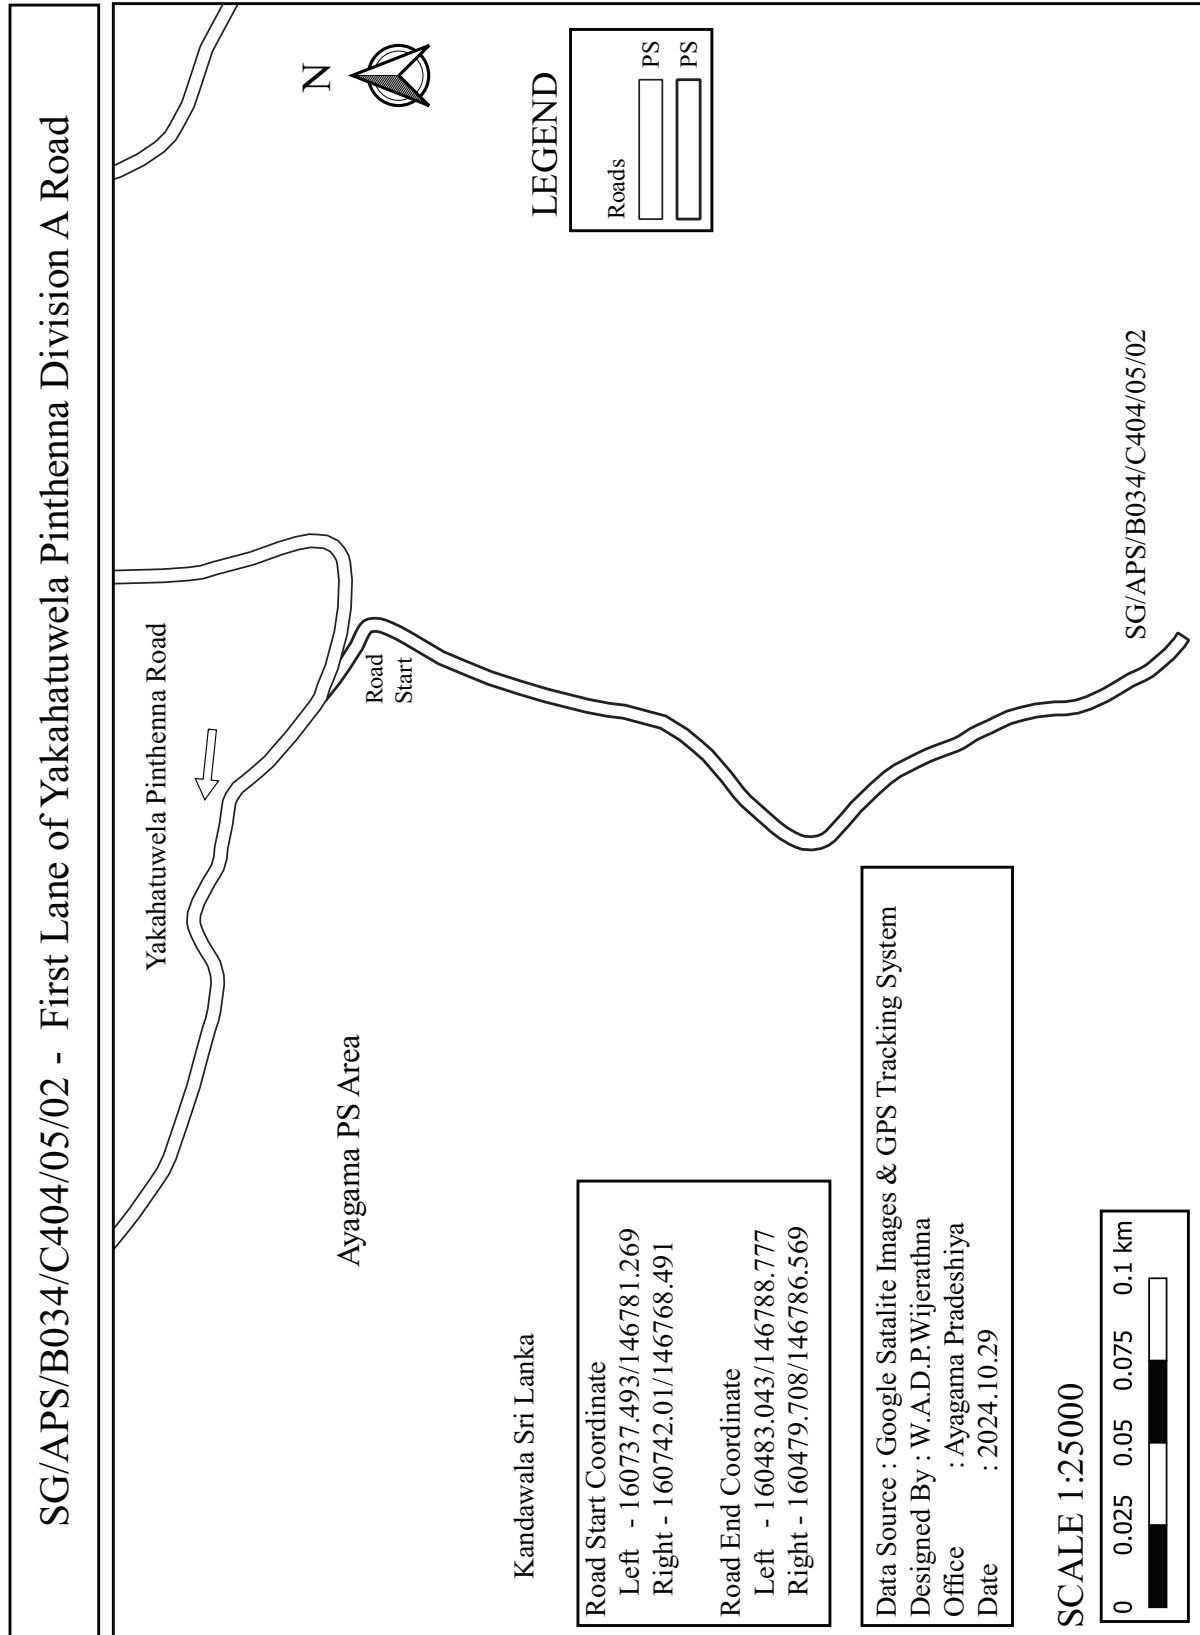


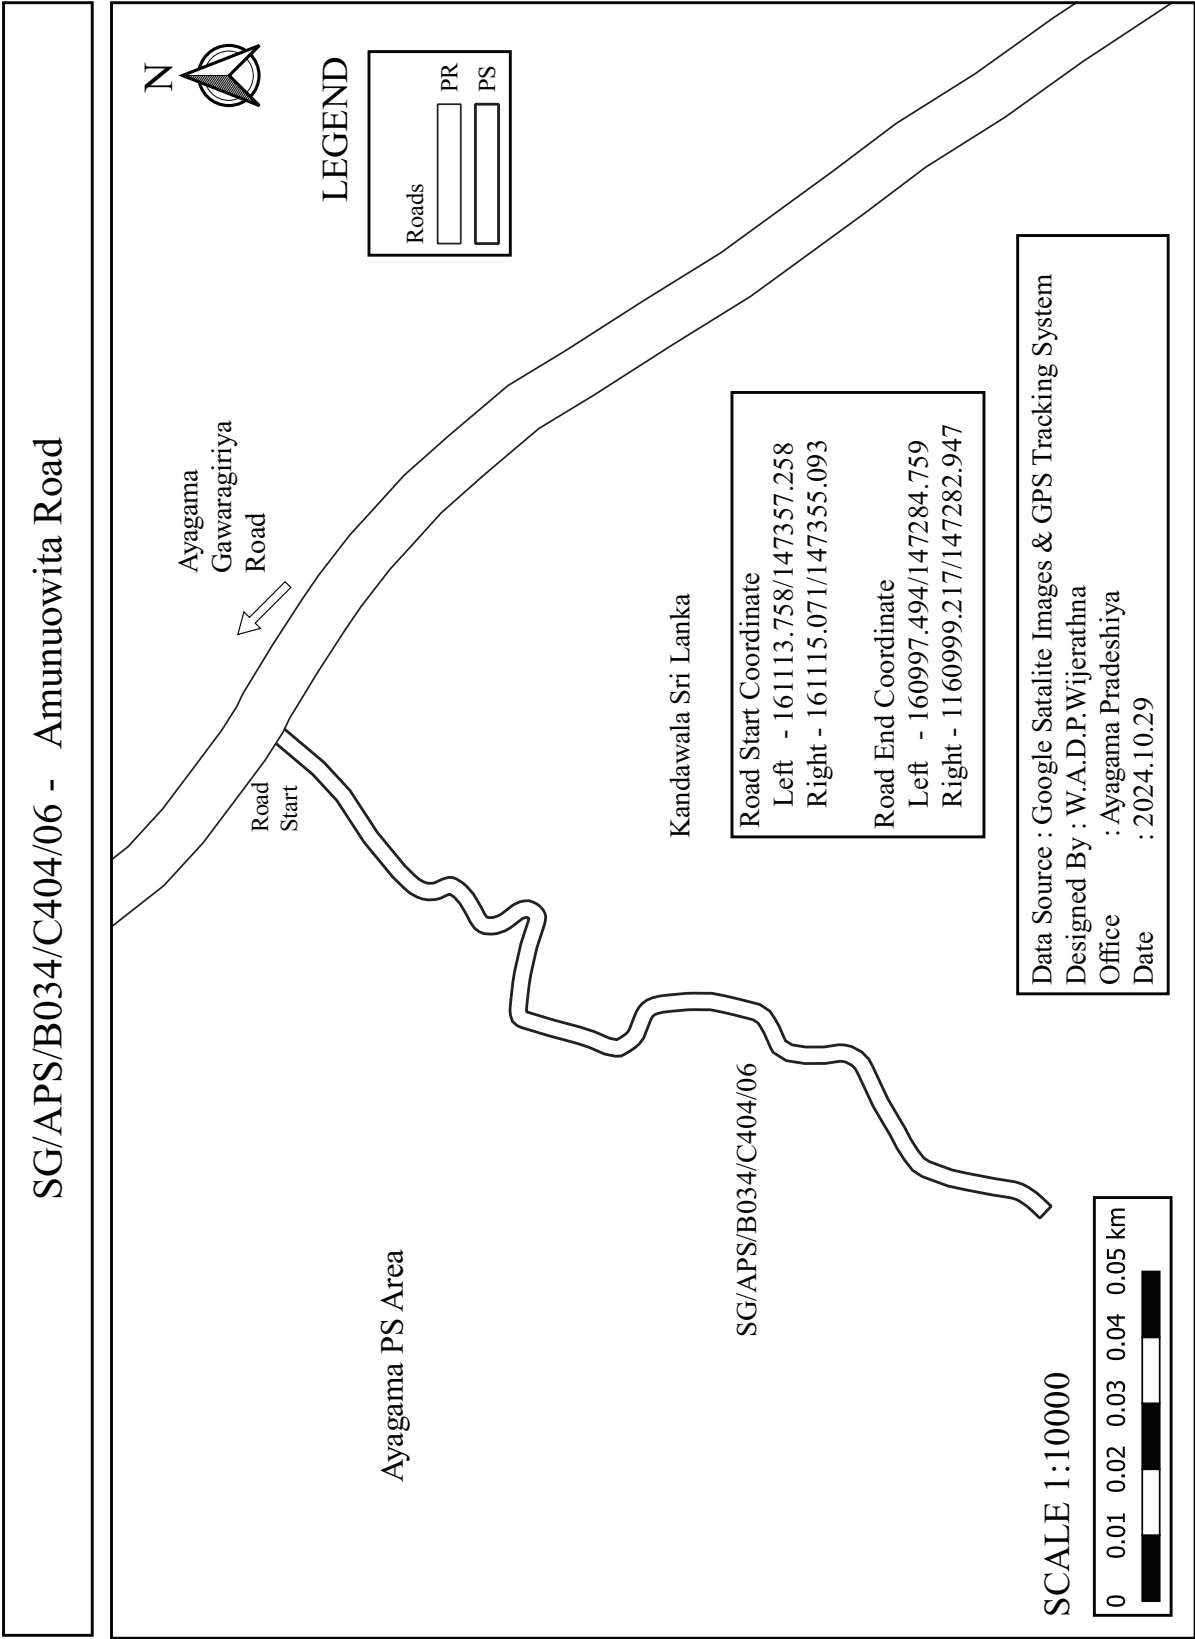


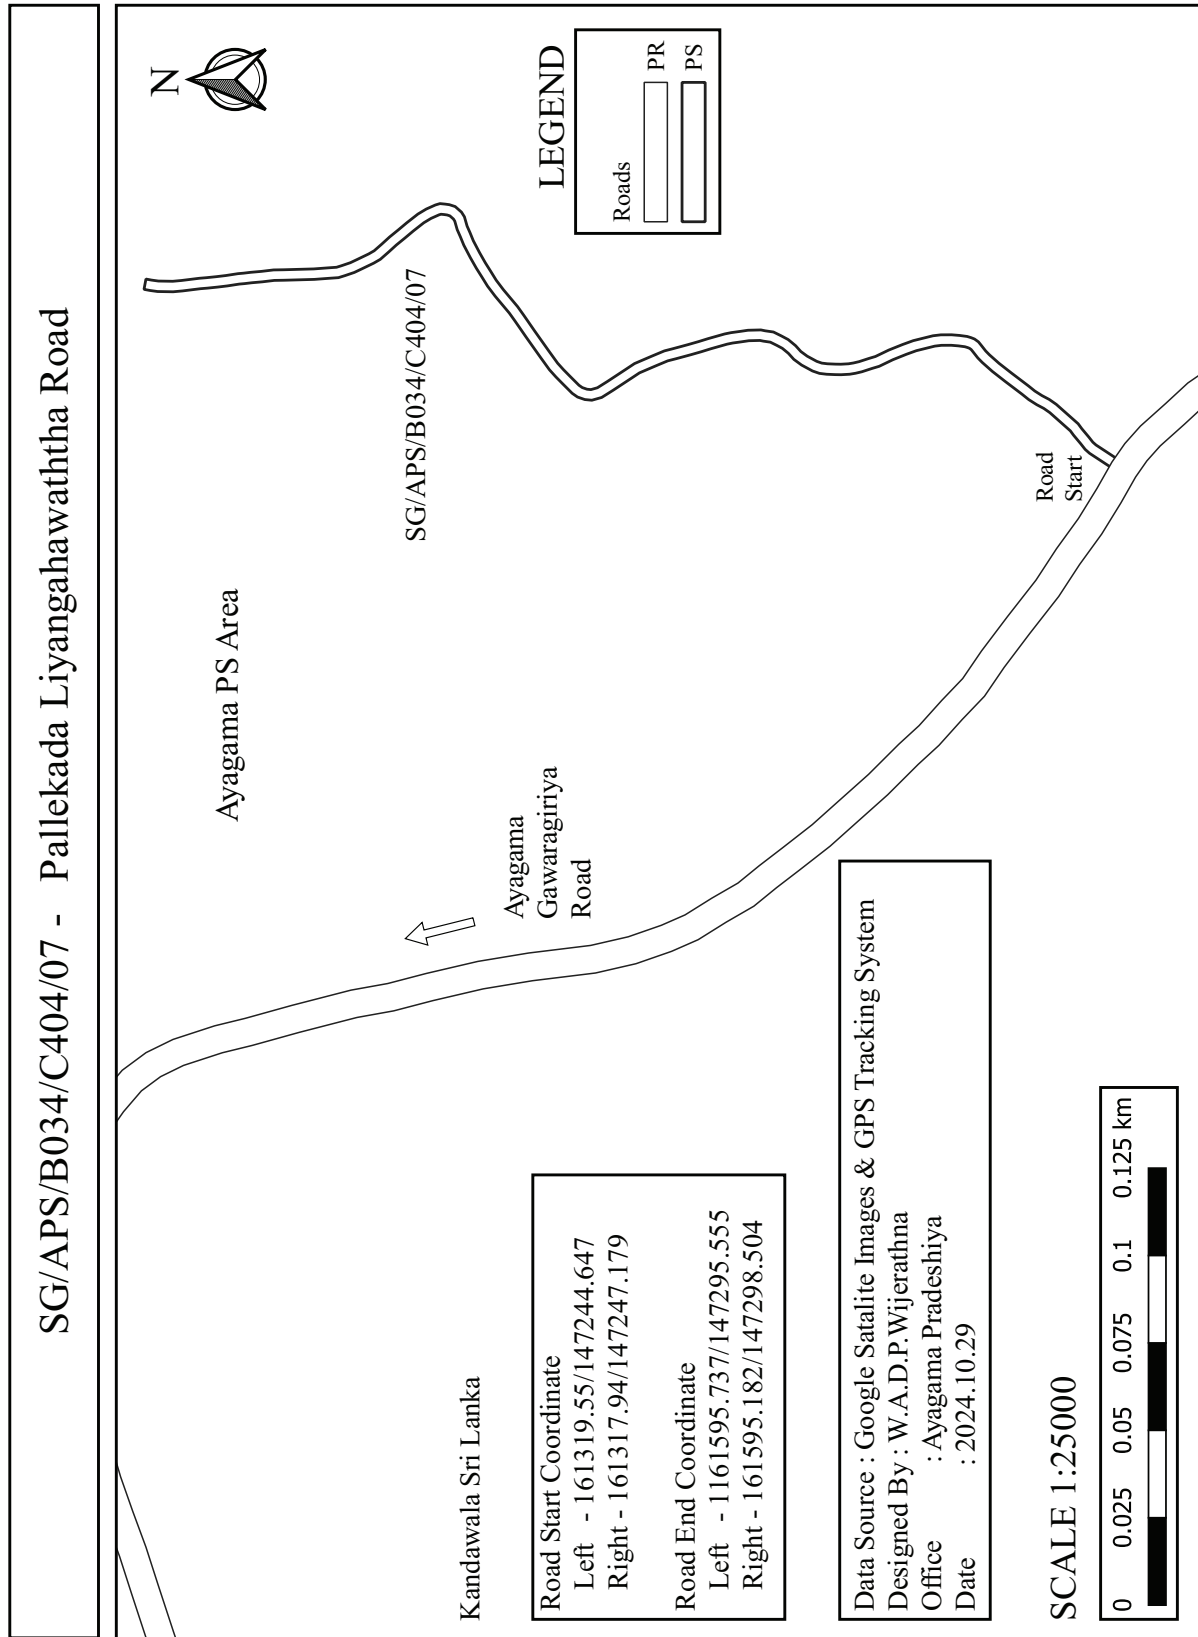


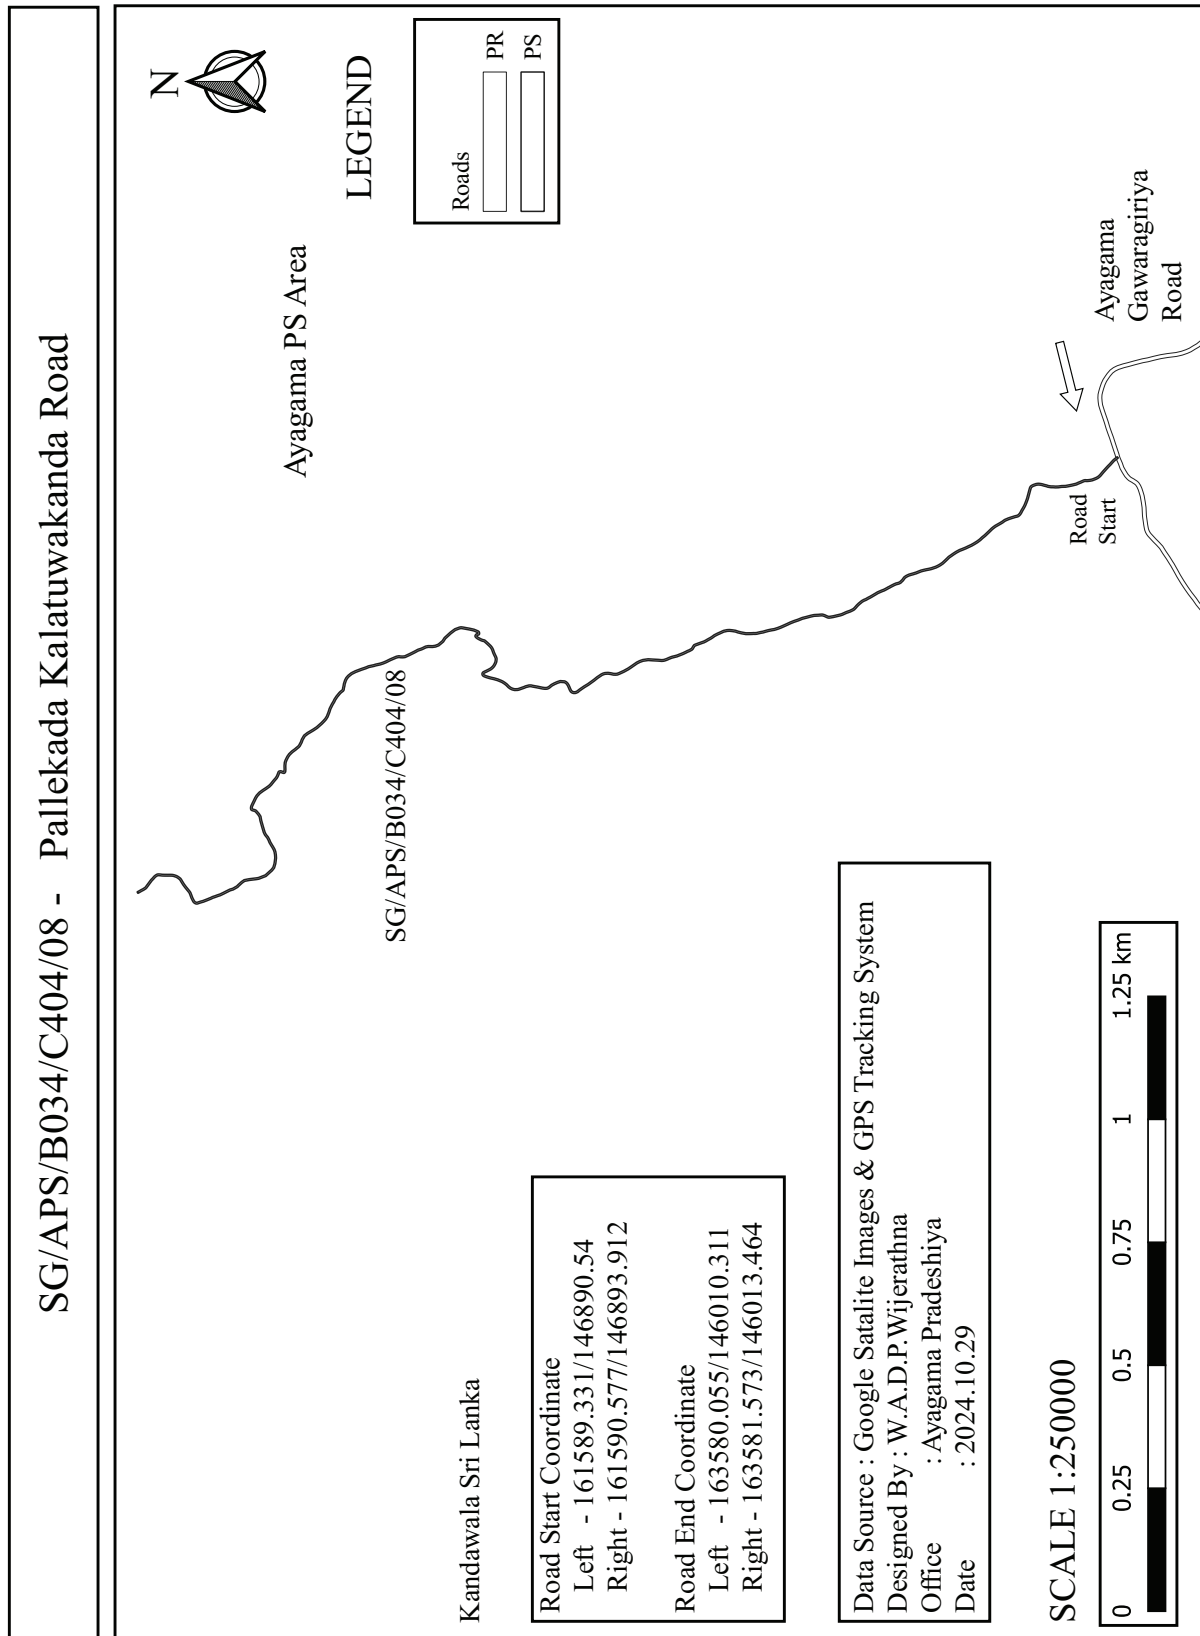





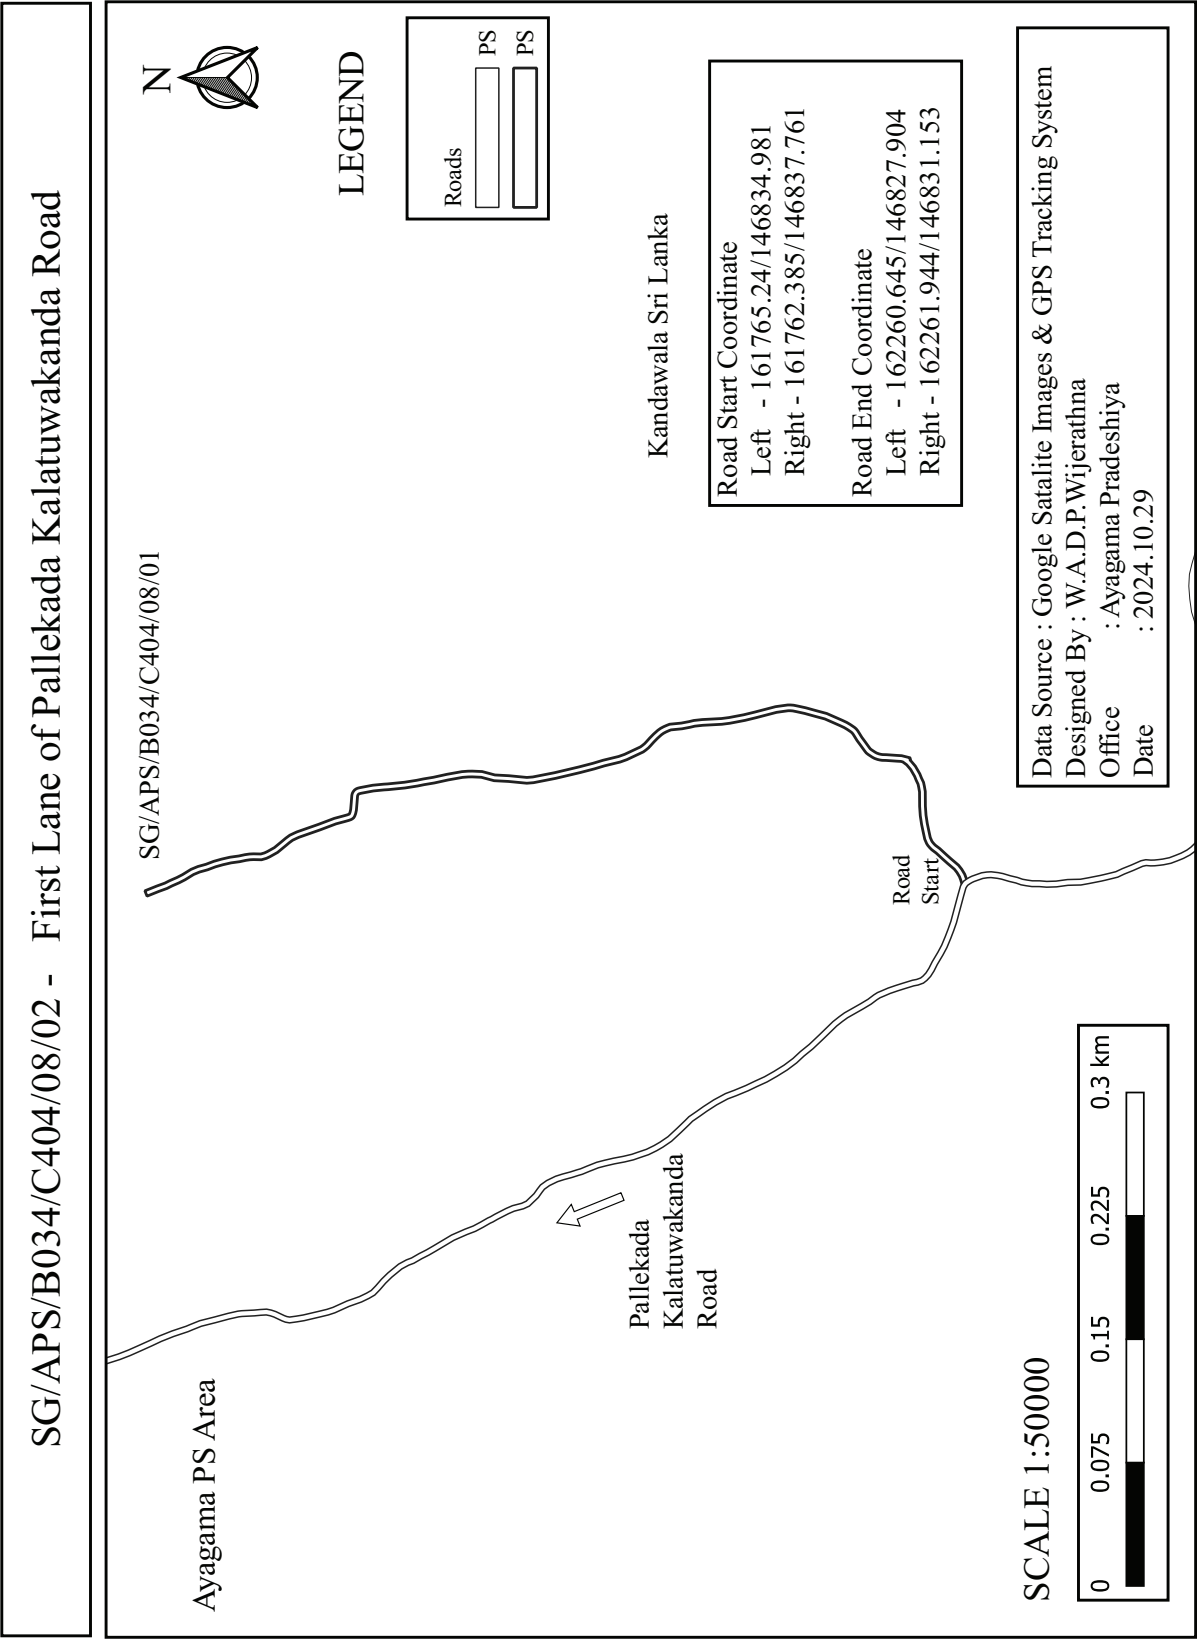


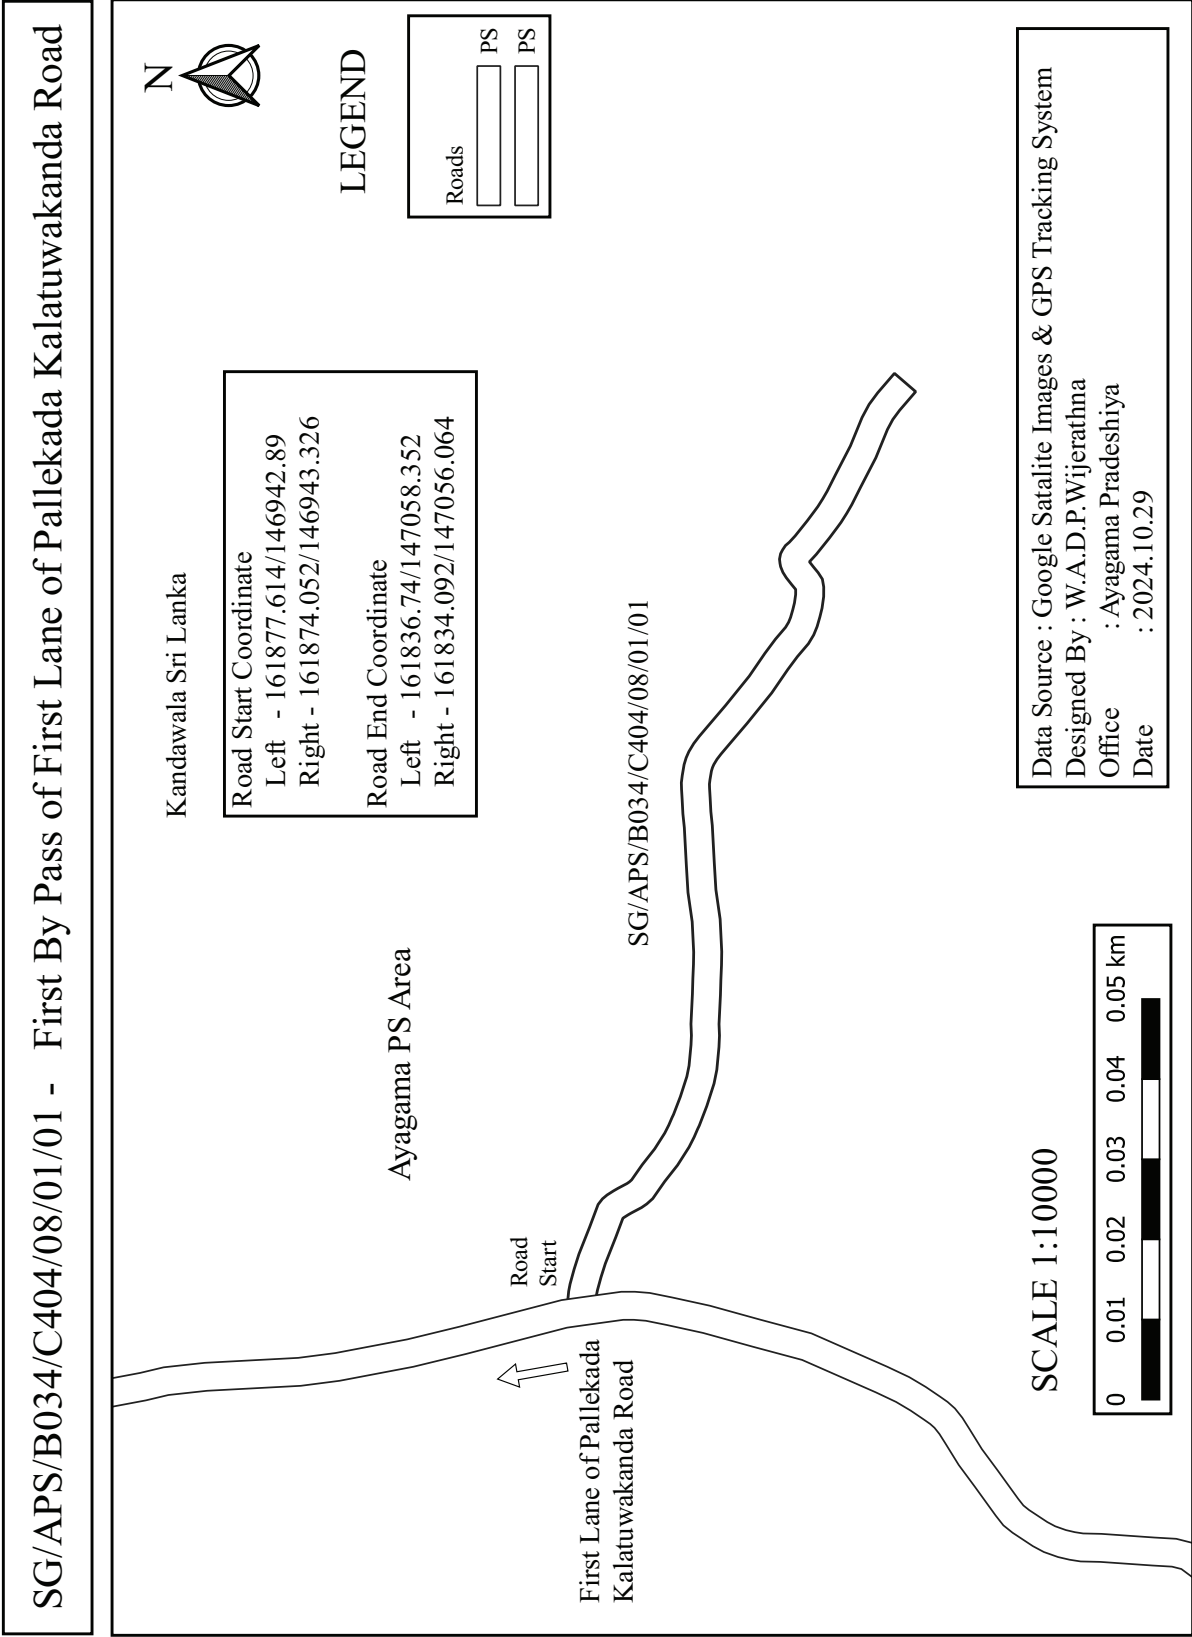


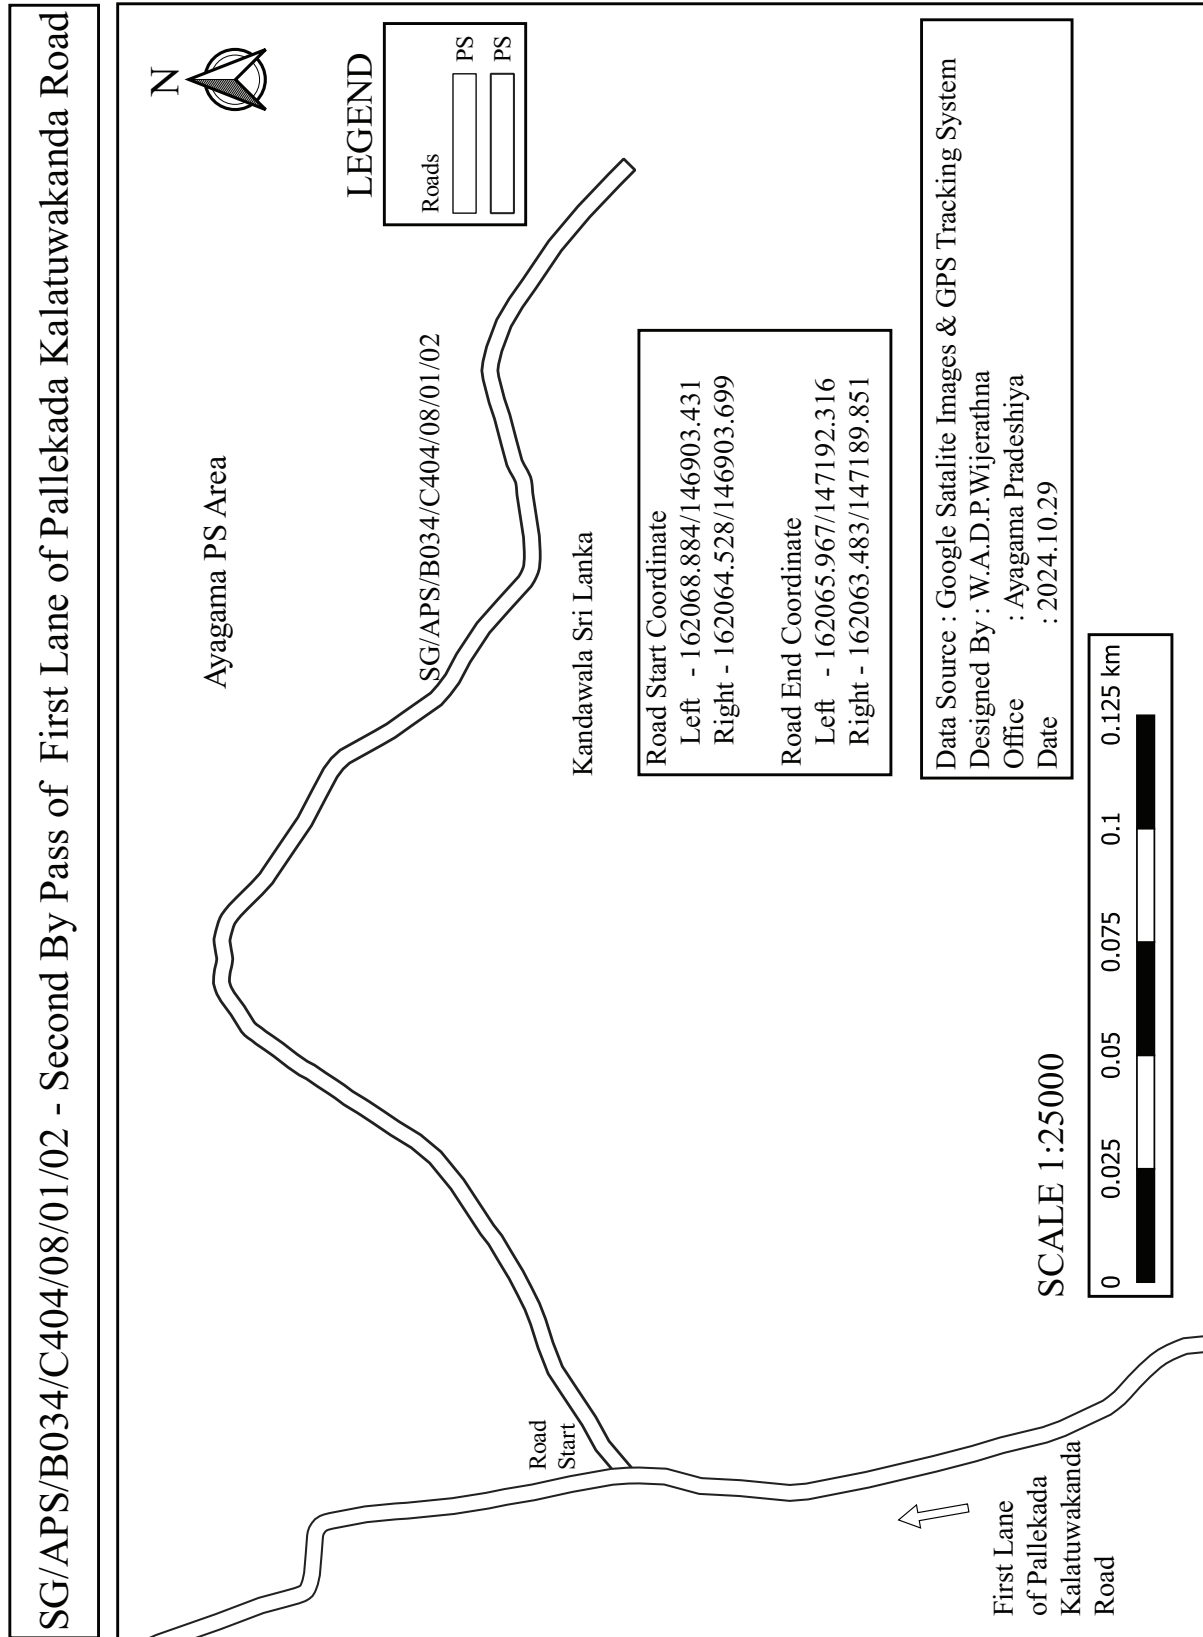


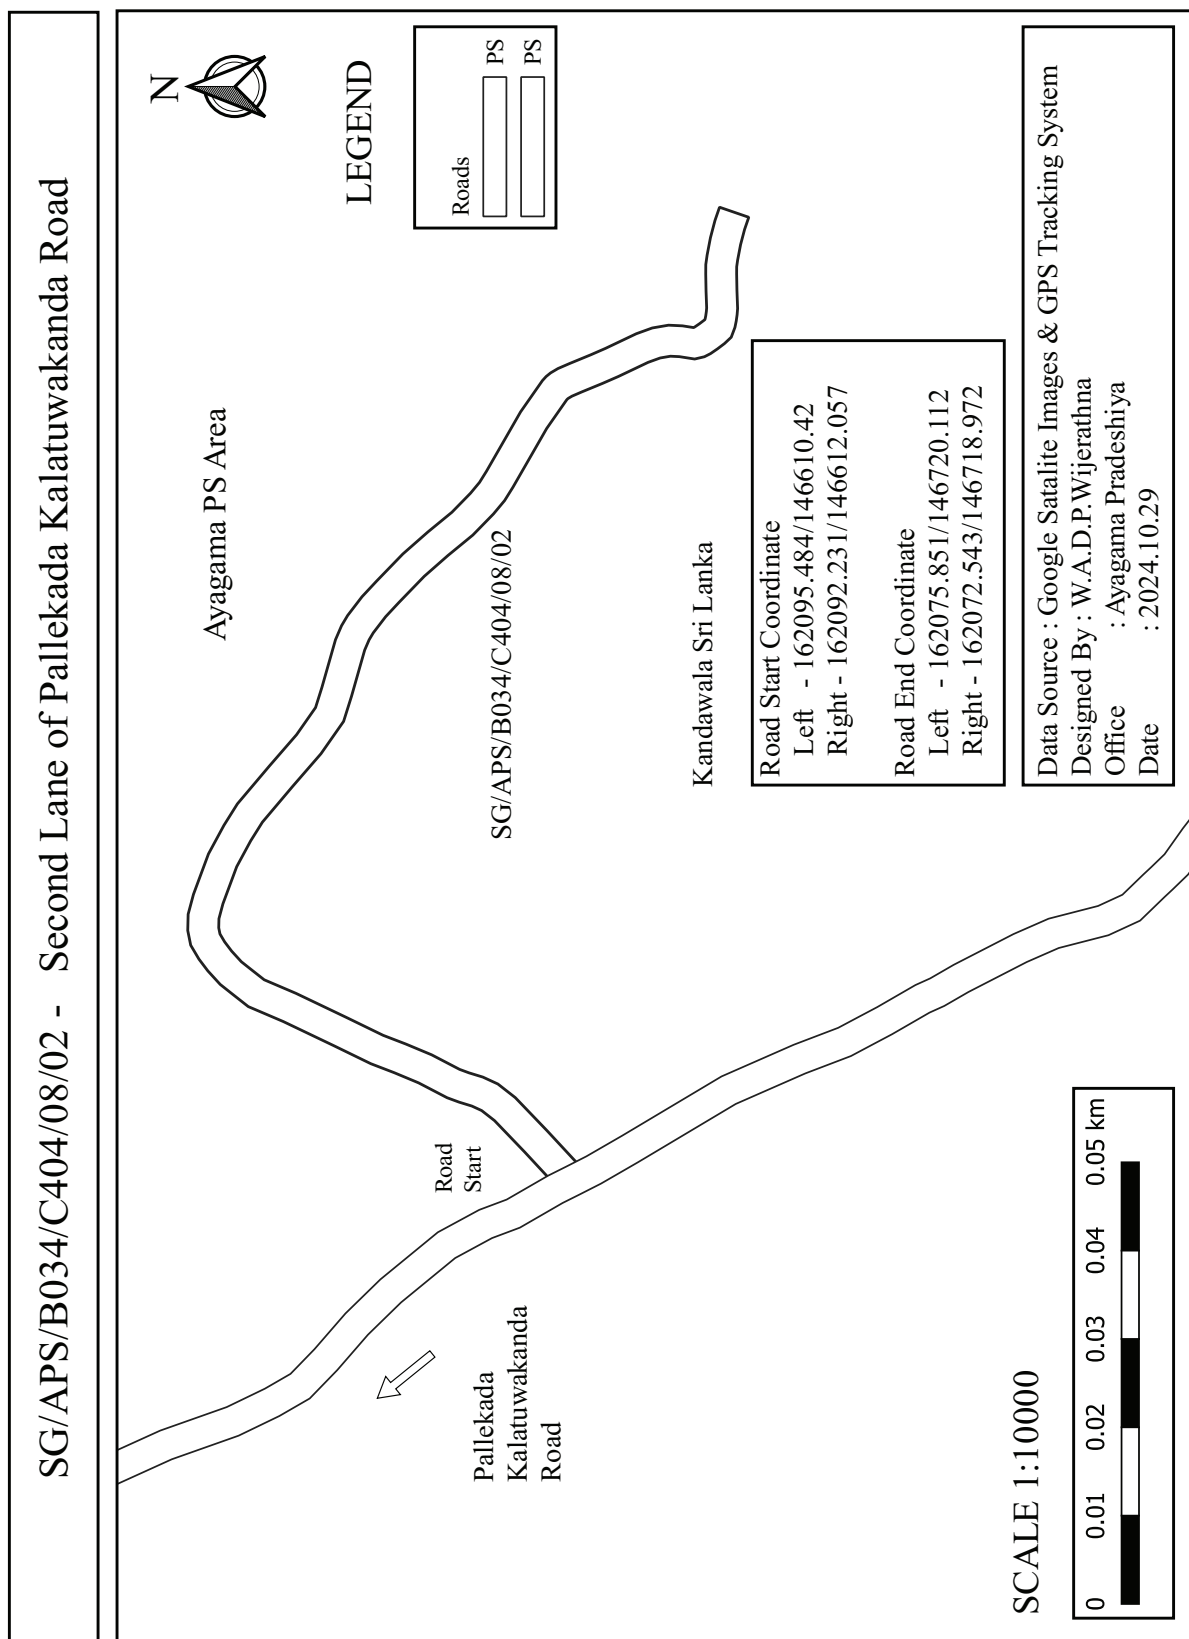

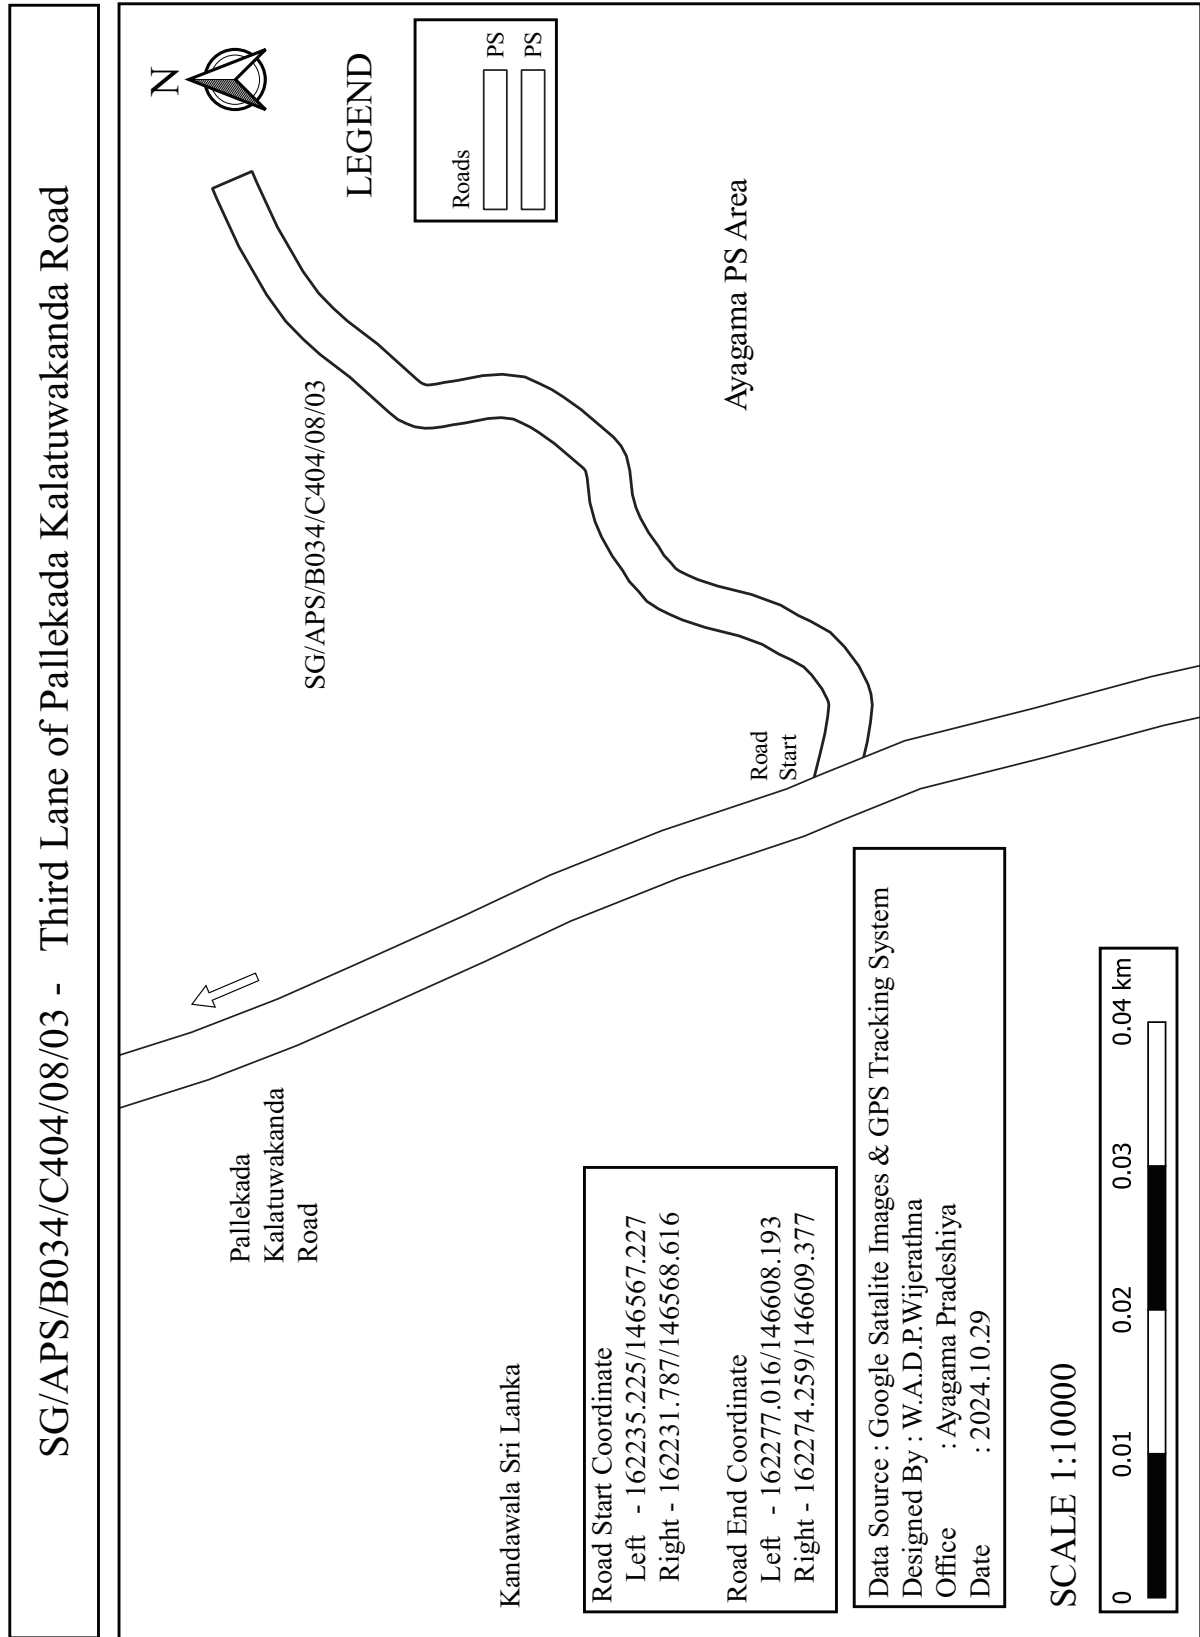

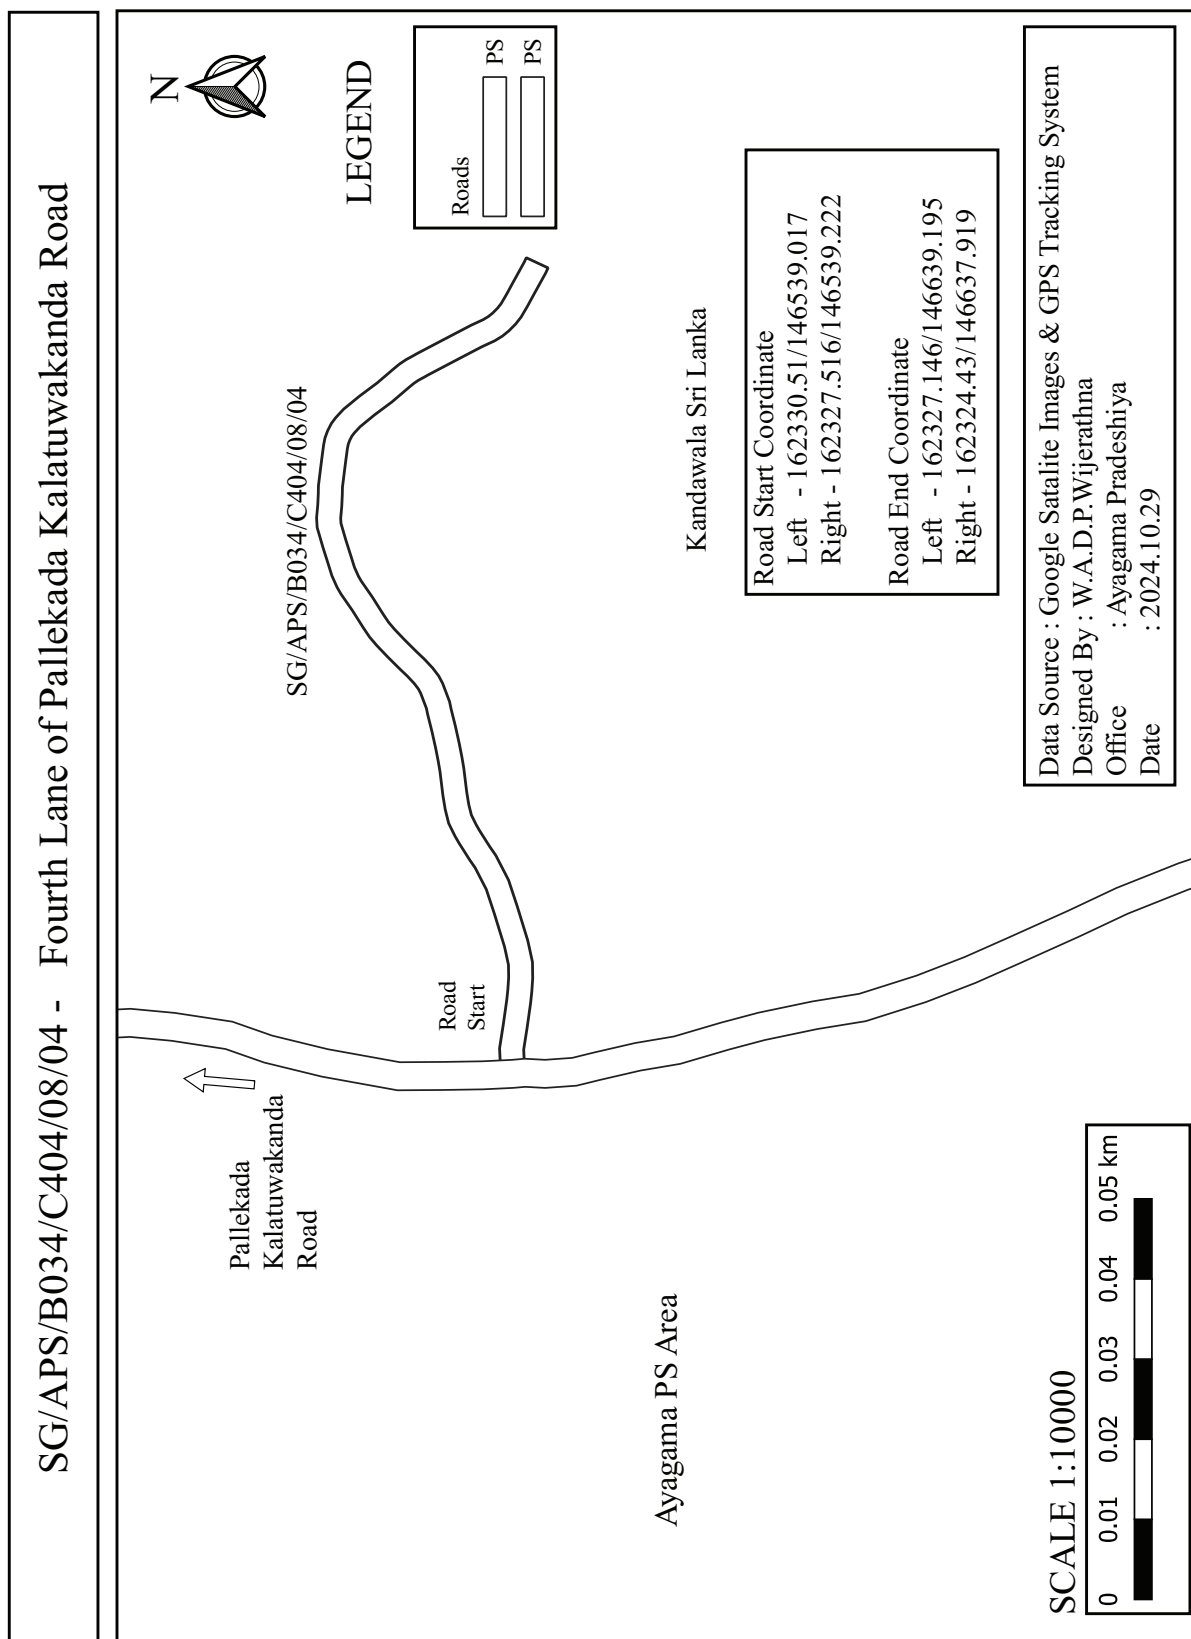

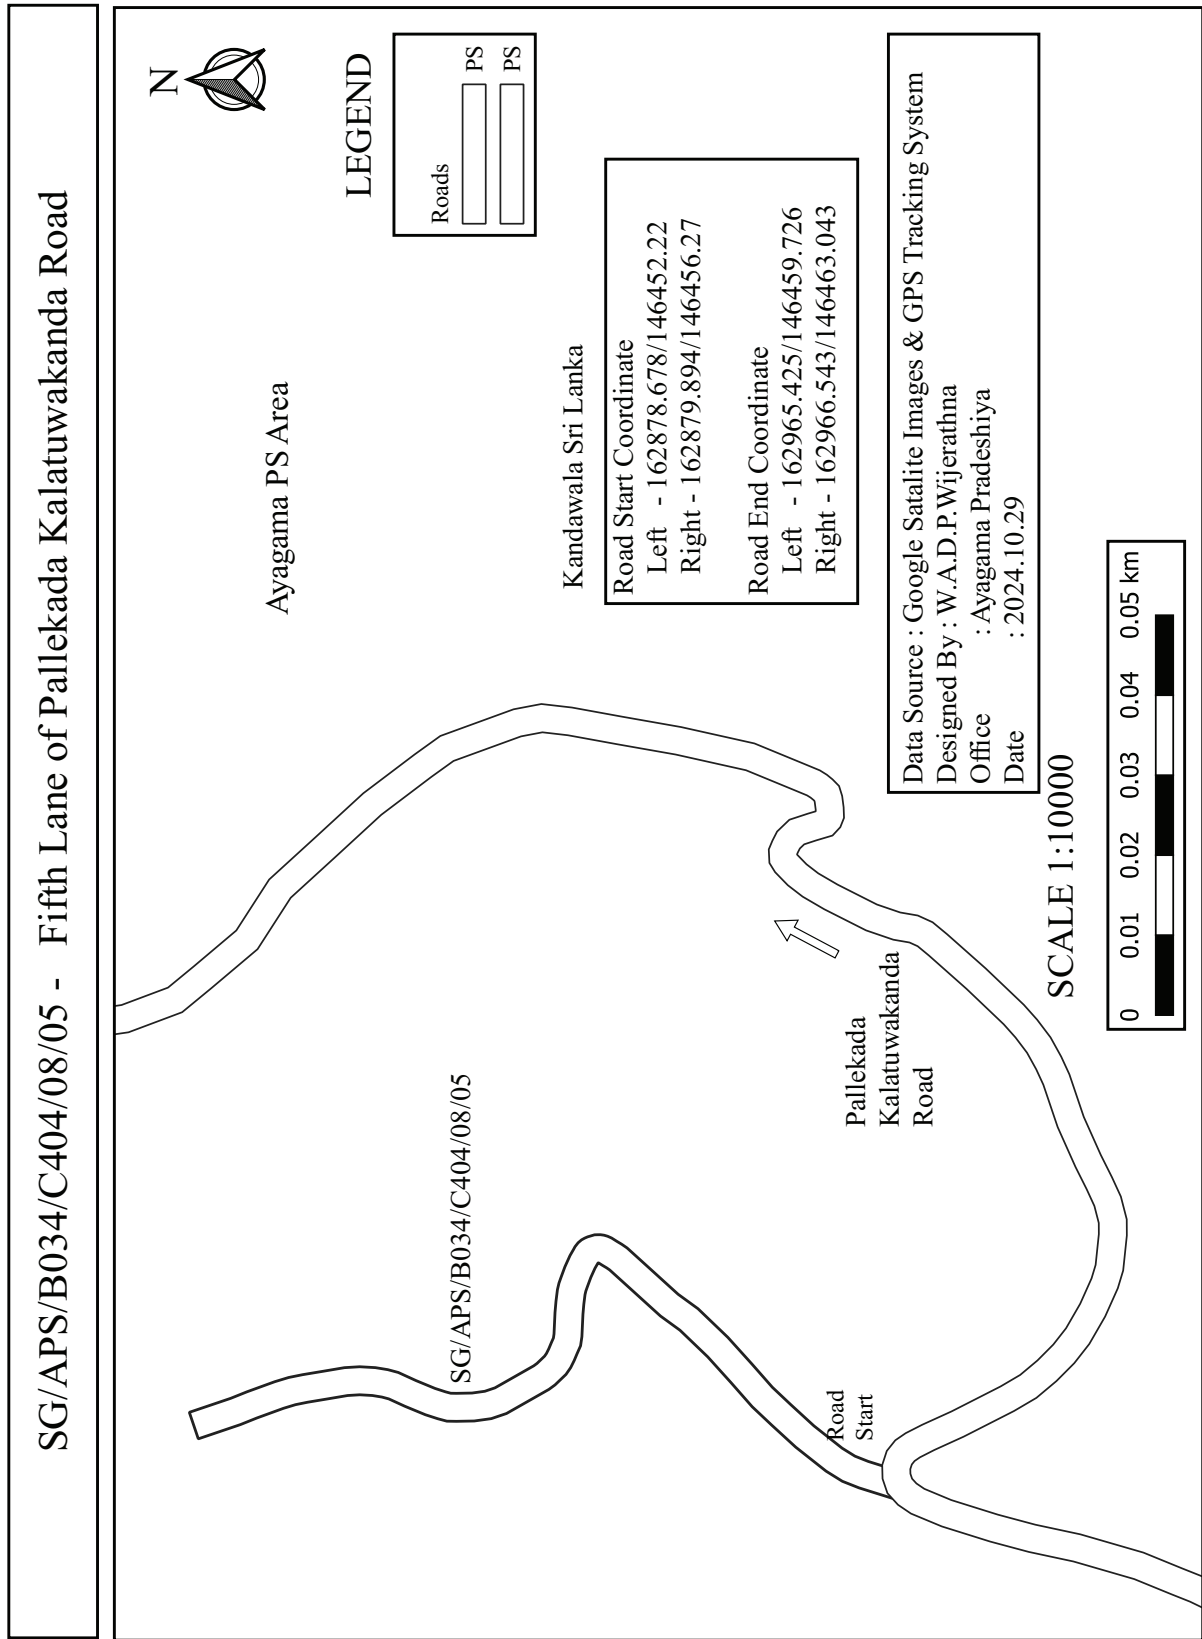

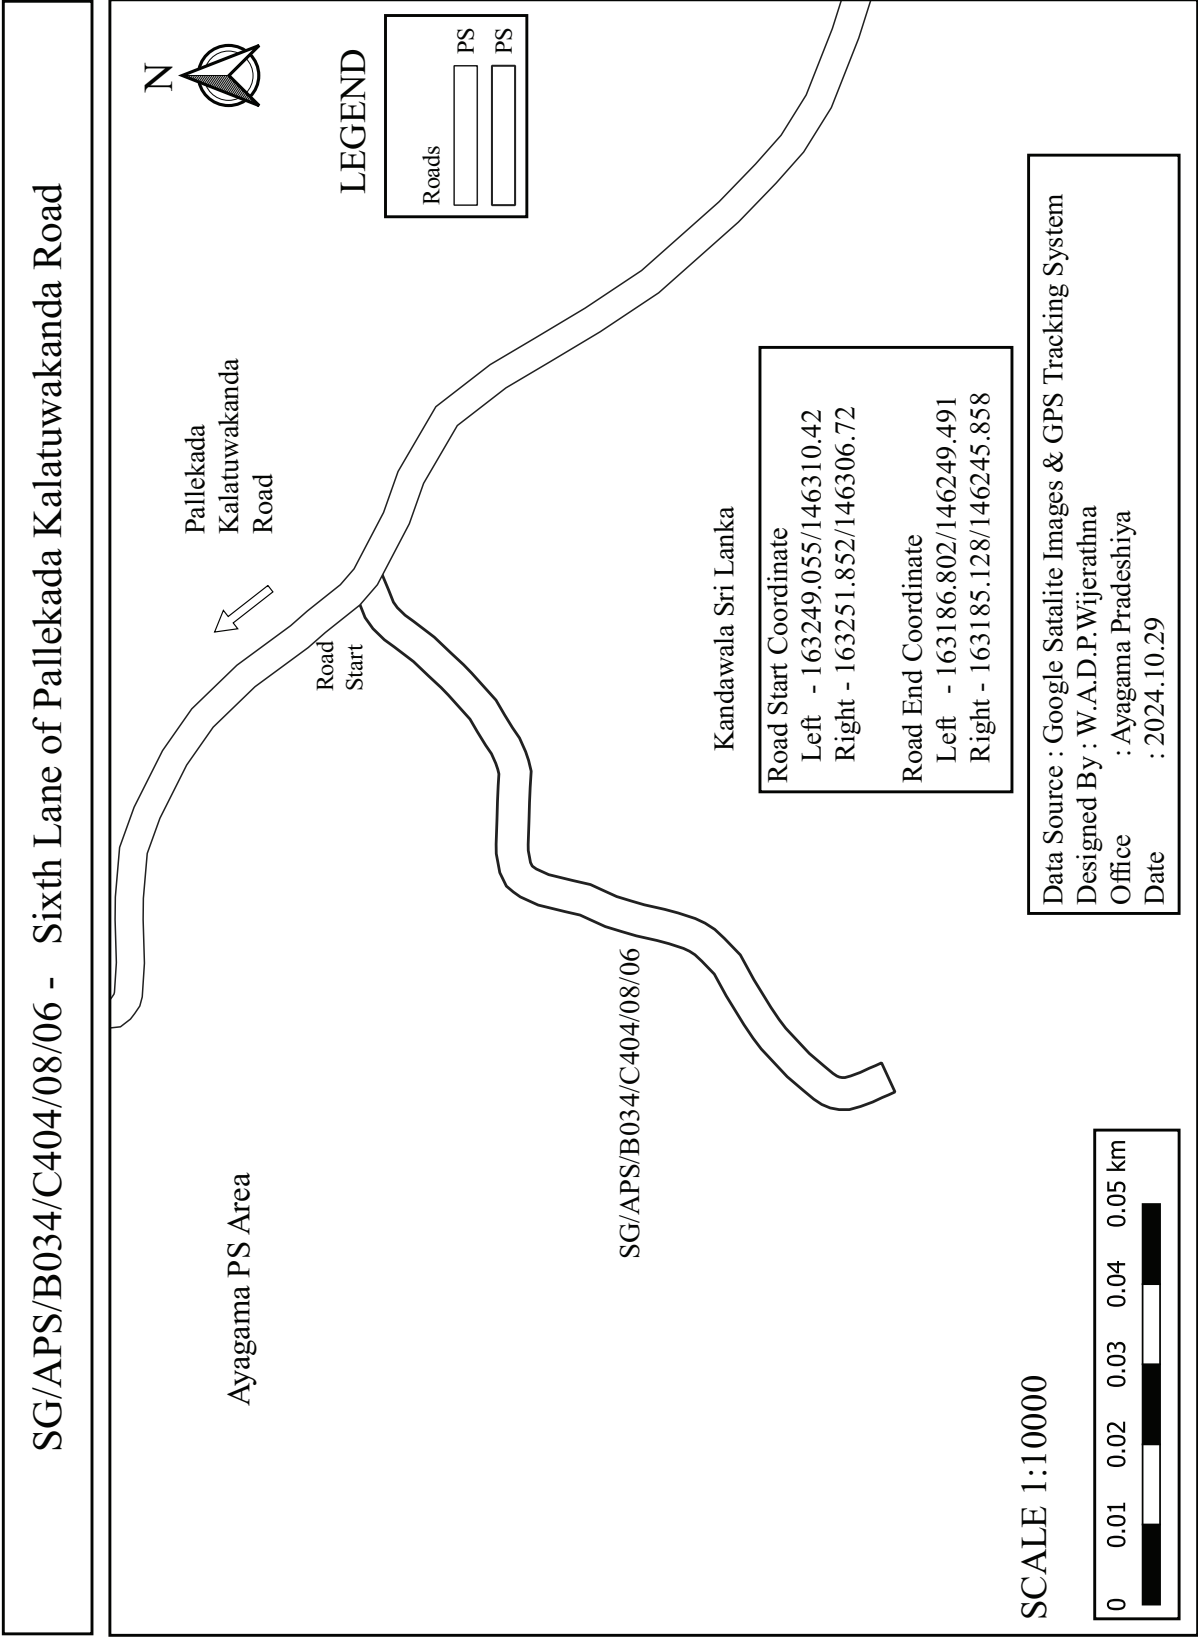



SG/APS/B034/C404/08/07 - Seventh Lane of Pallekada Kalatuwakanda Road

Kandawala Sri Lanka

Road Start Coordinate

Left - 163349.292/146179.163

Right - 163350.69/146182.28

Road End Coordinate

Left - 163466.236/146261.559

Right - 163469.087/146263.589

Ayagama PS Area

SG/APS/B034/C404/08/07



LEGEND

Roads

PS

PS


Data Source : Google Satalite Images & GPS Tracking System

Designed By : W.A.D.P.Wijerathna

Office : Ayagama Pradeshiya

Date : 2024.10.29


SCALE 1:25000

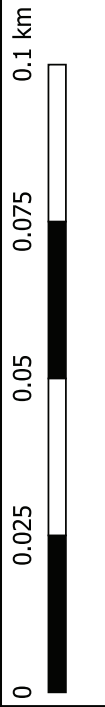



Road  
Start


Pallekada  
Kalatuwakanda  
Road




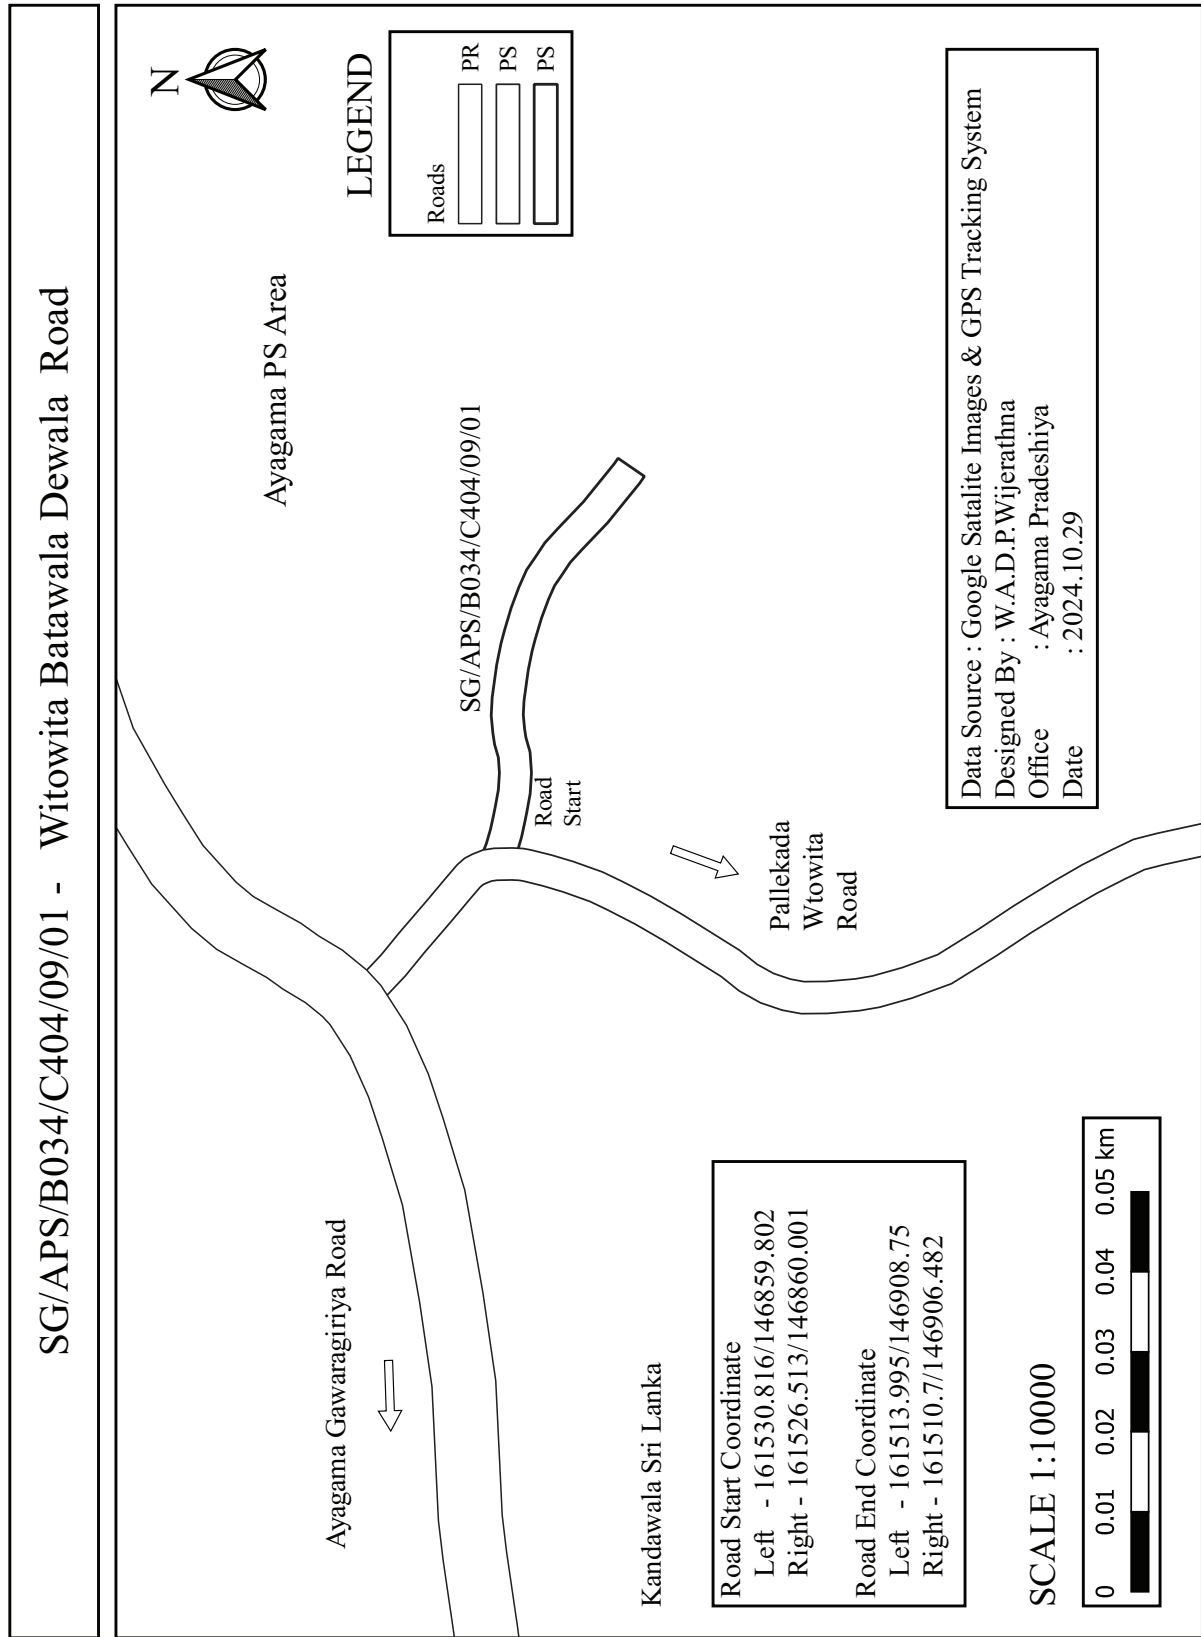


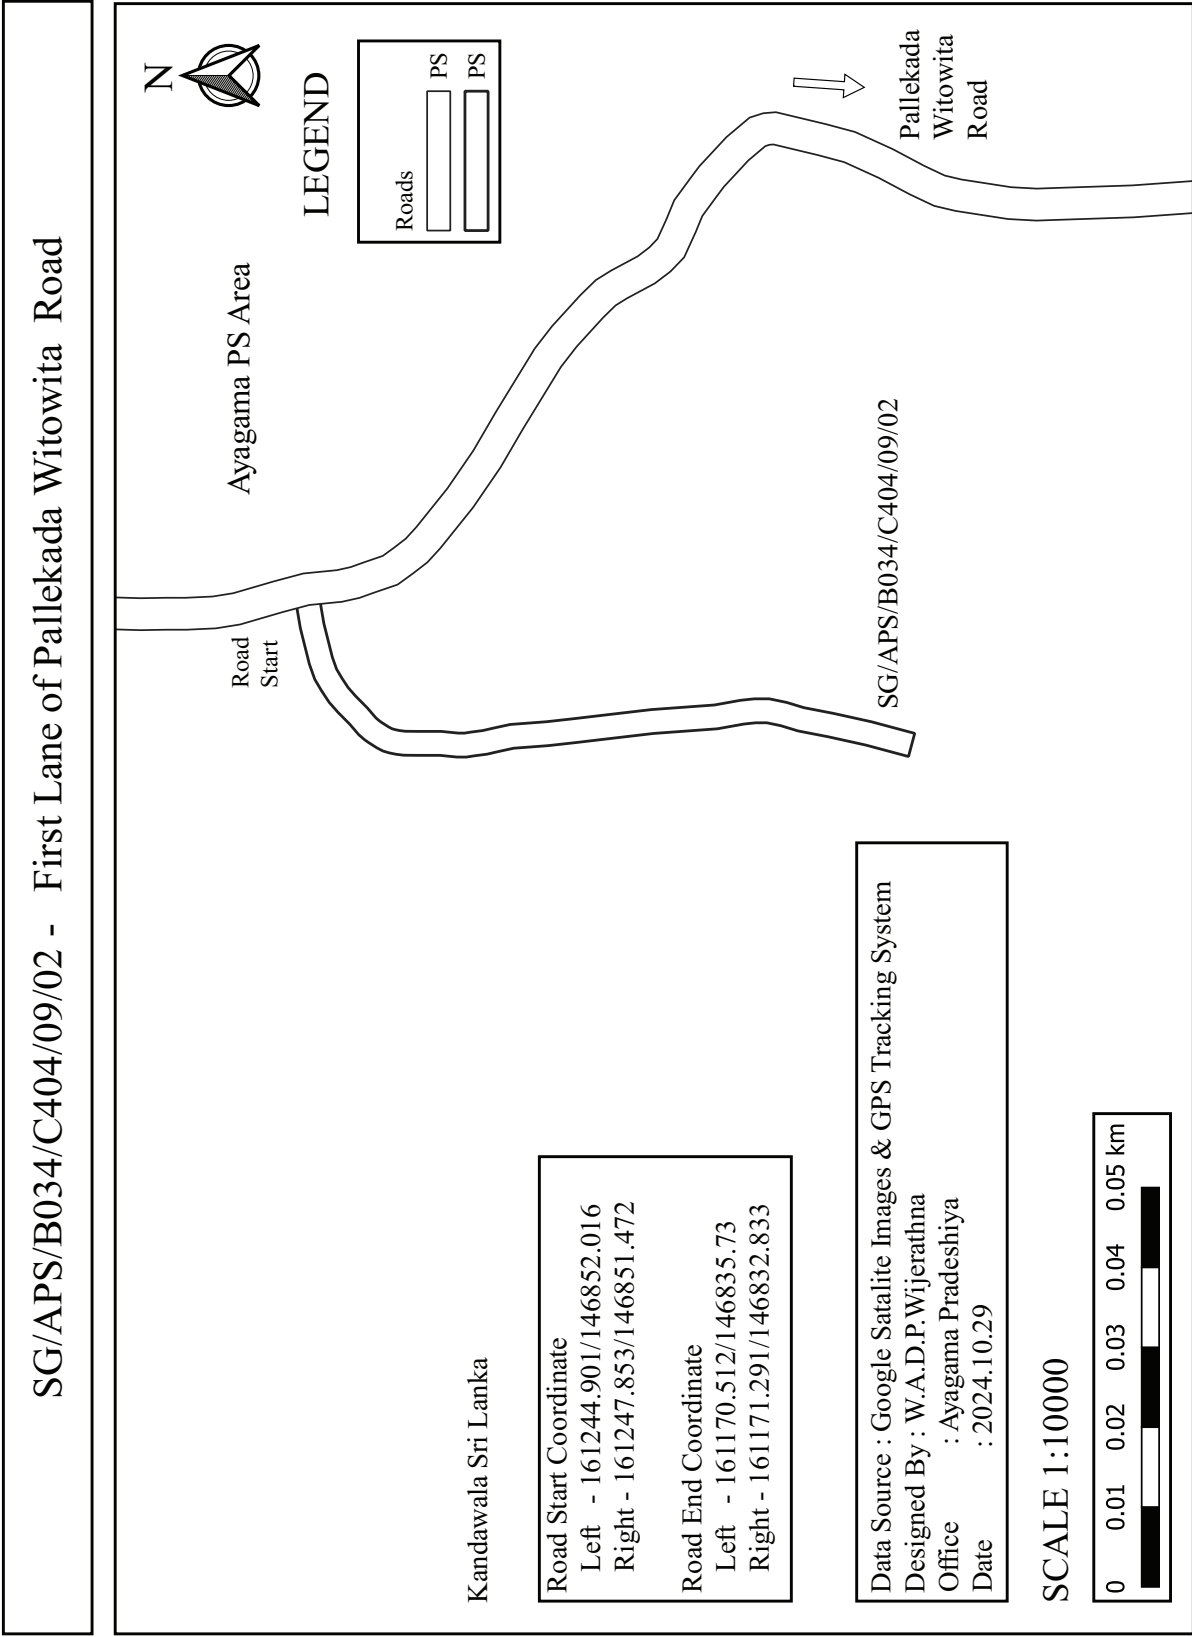

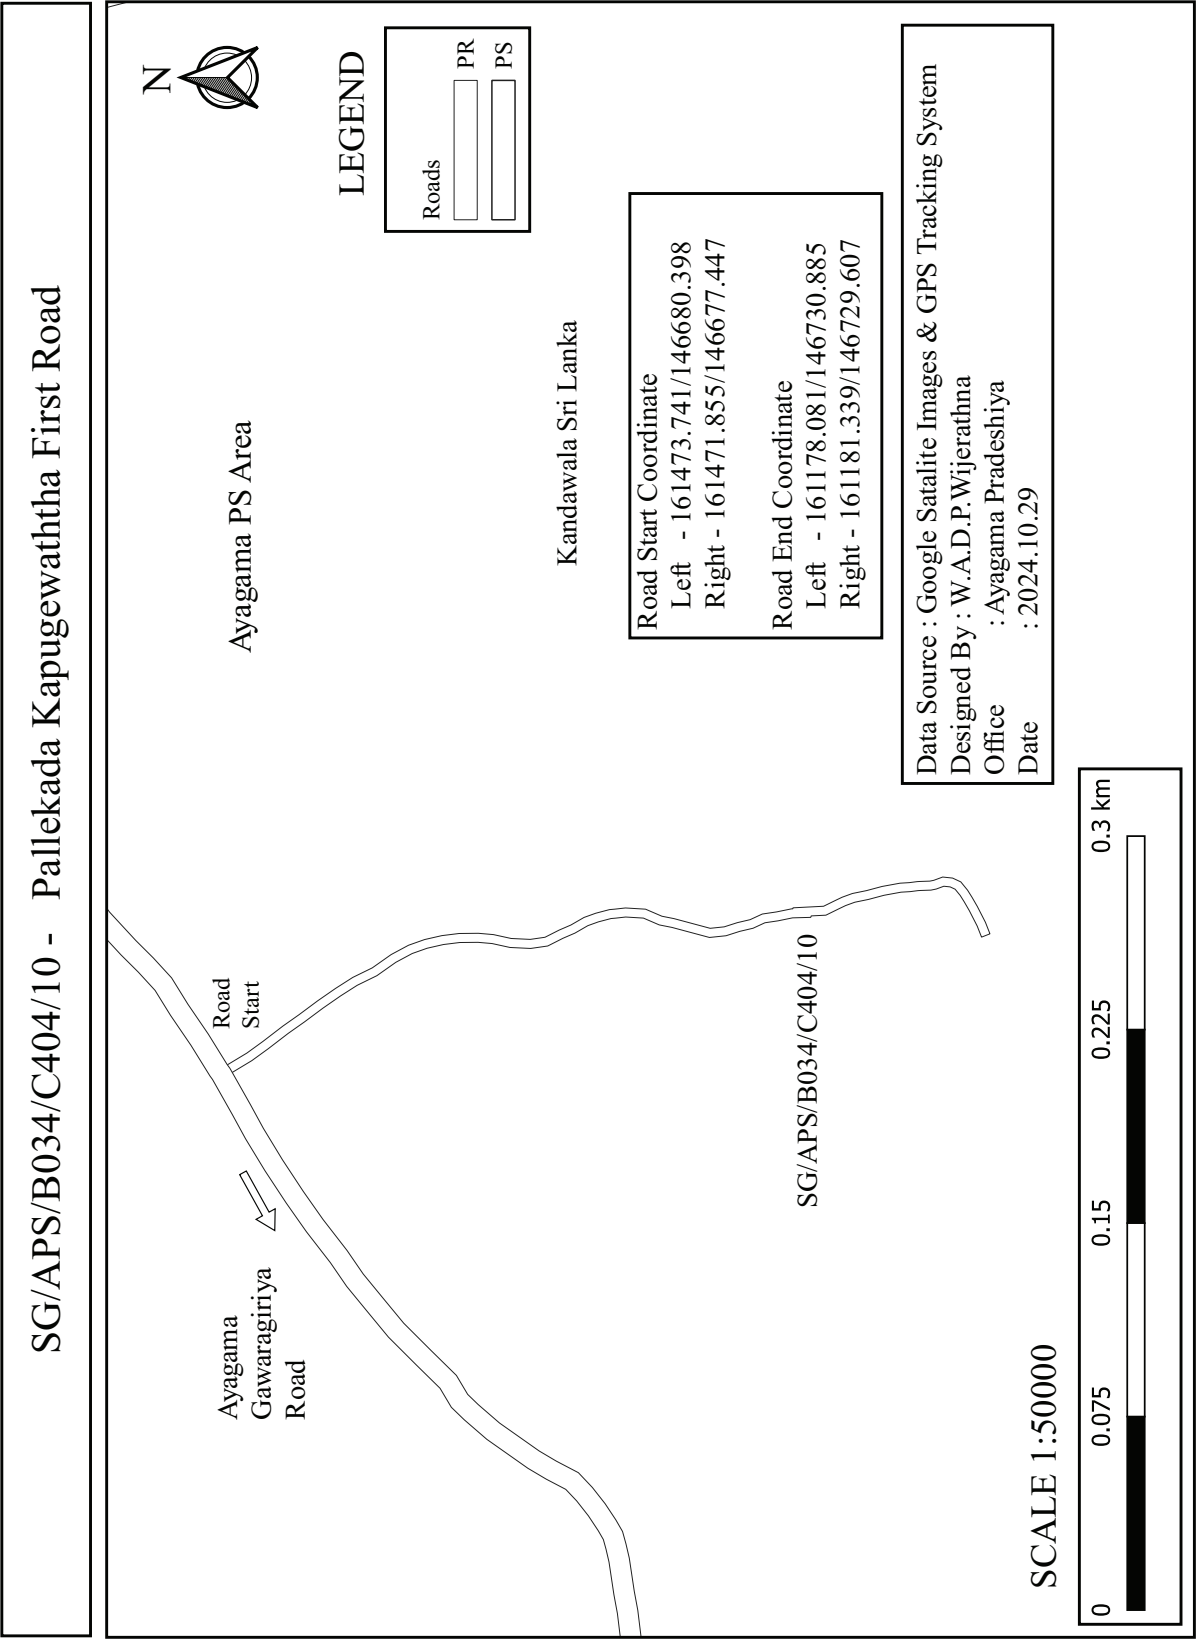


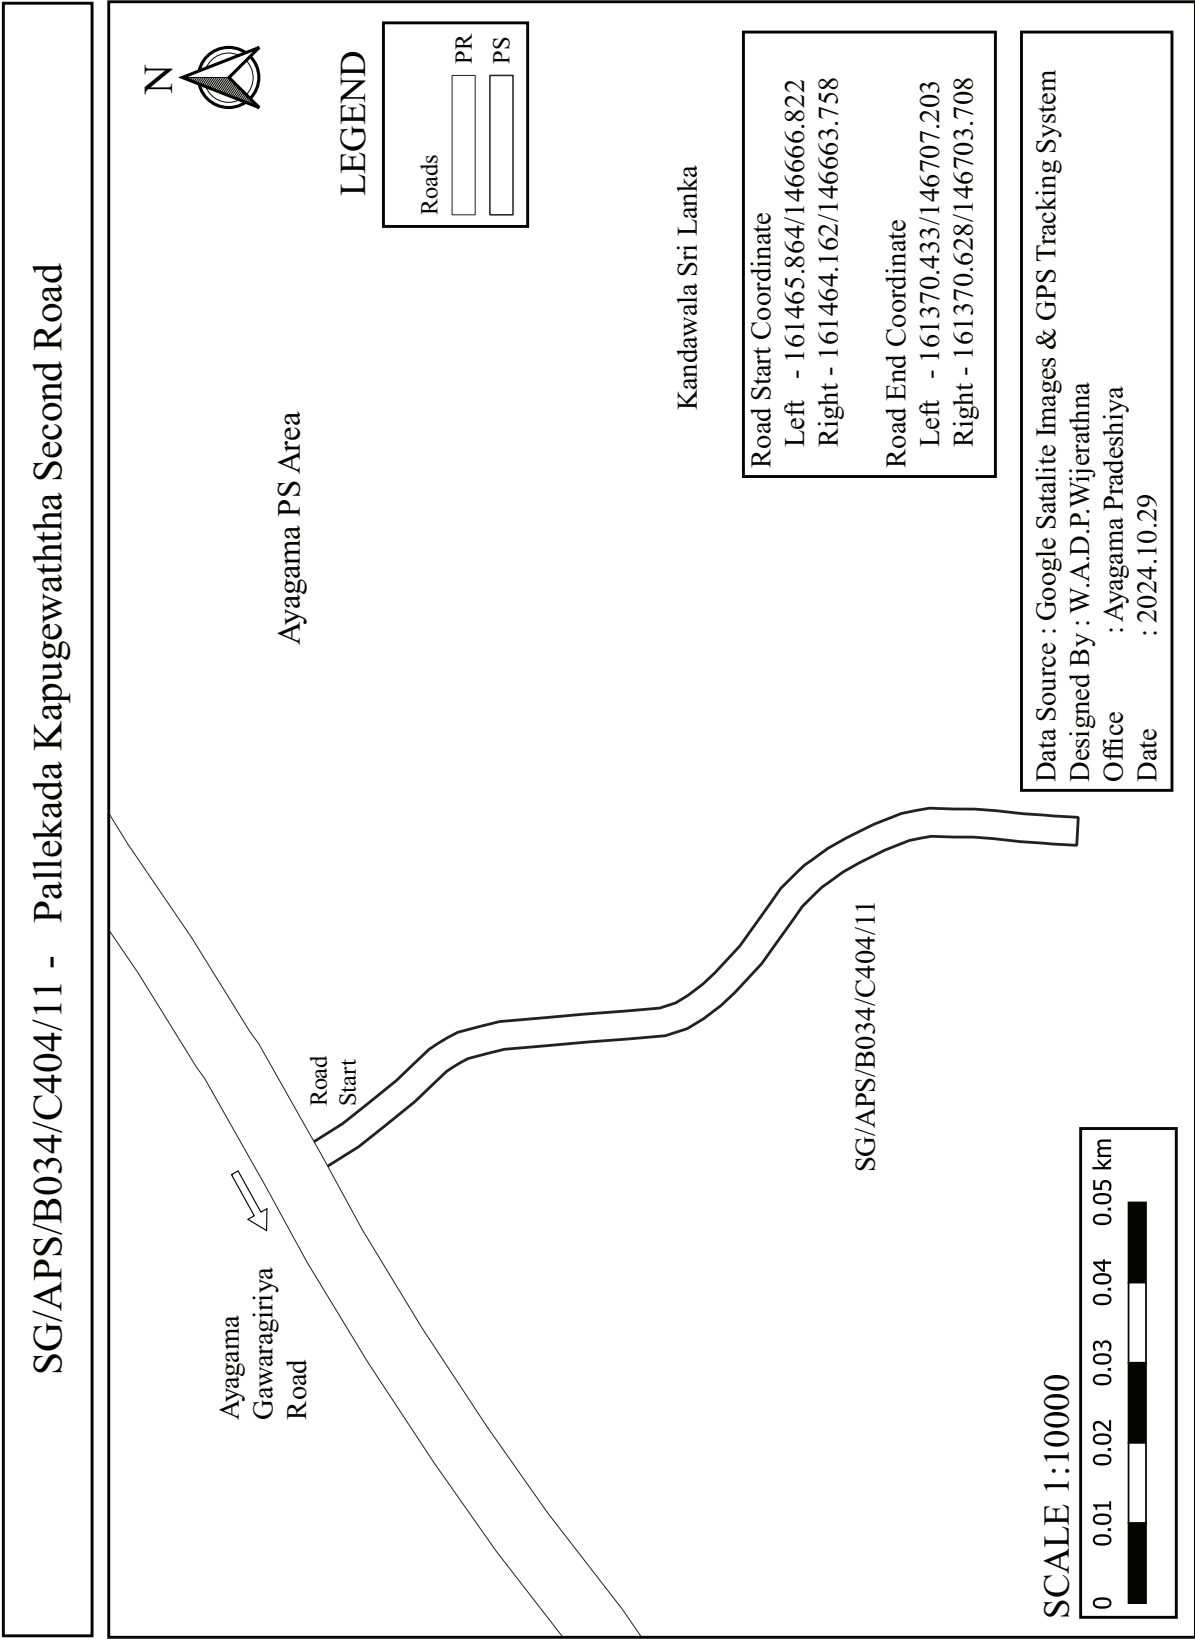


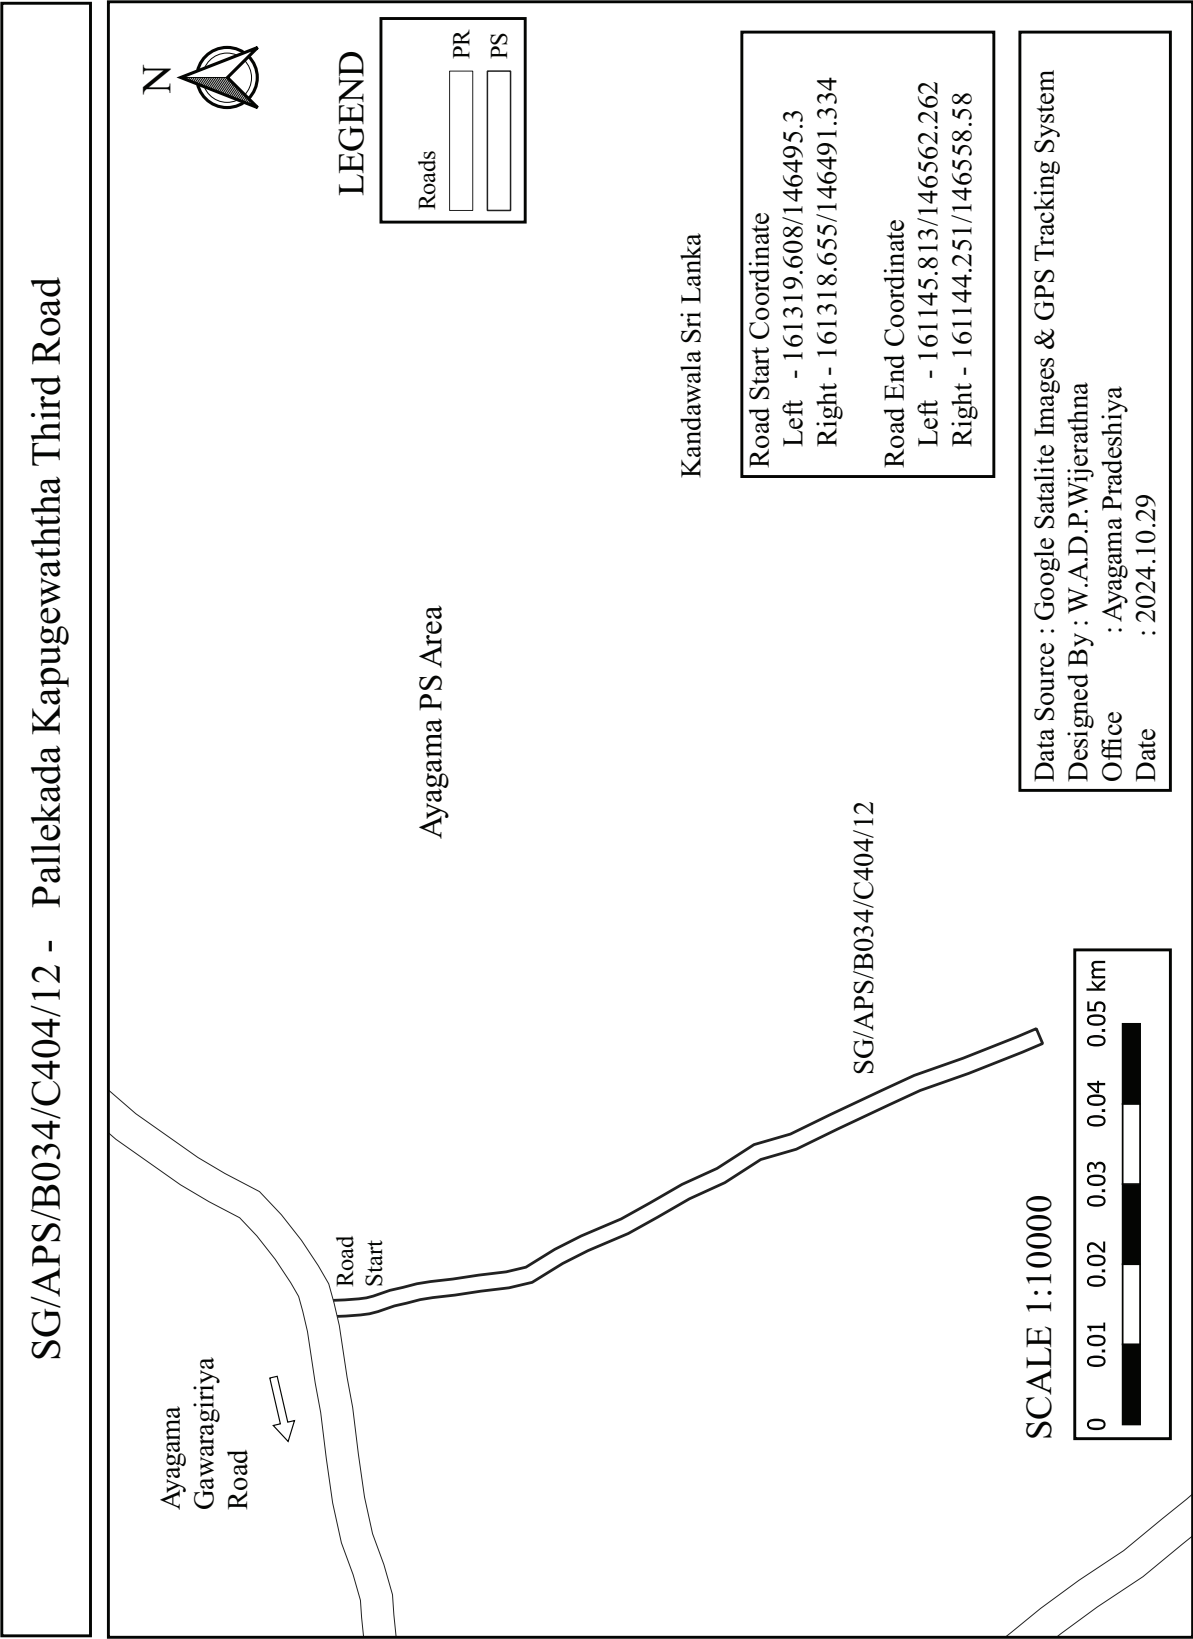


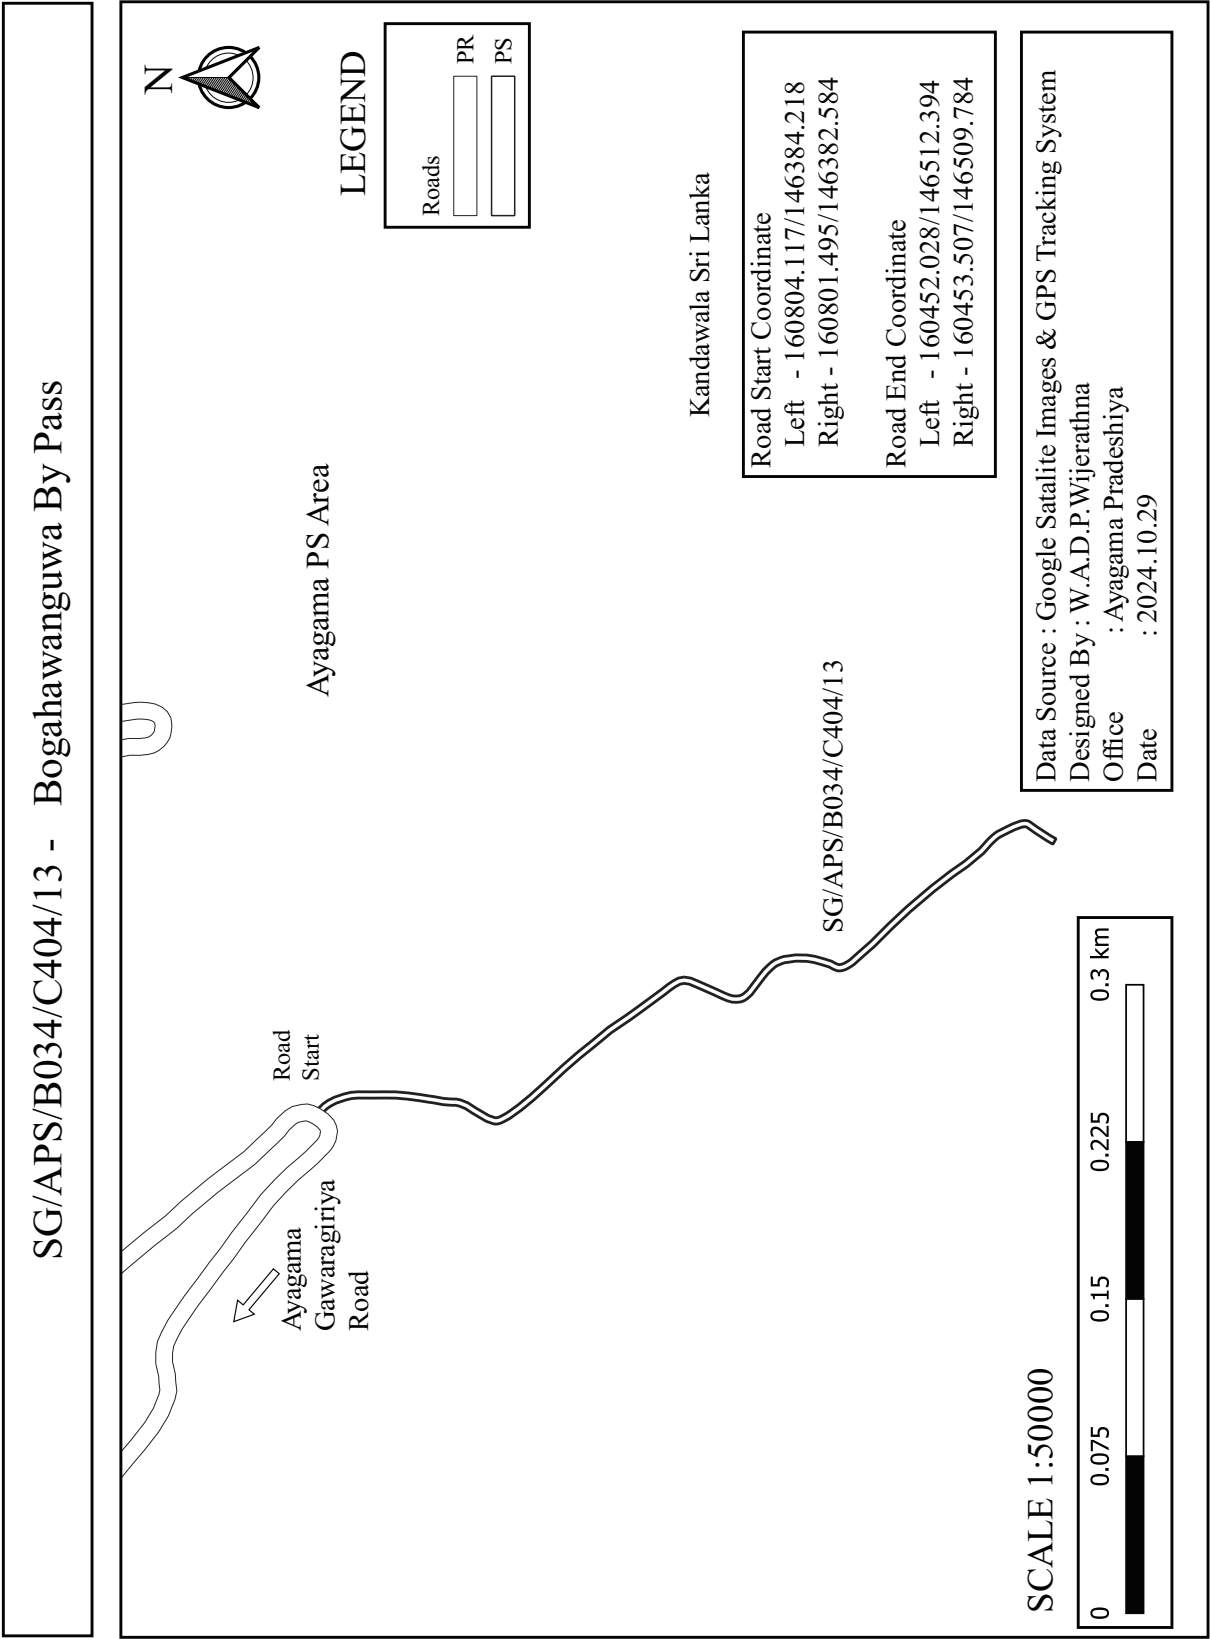





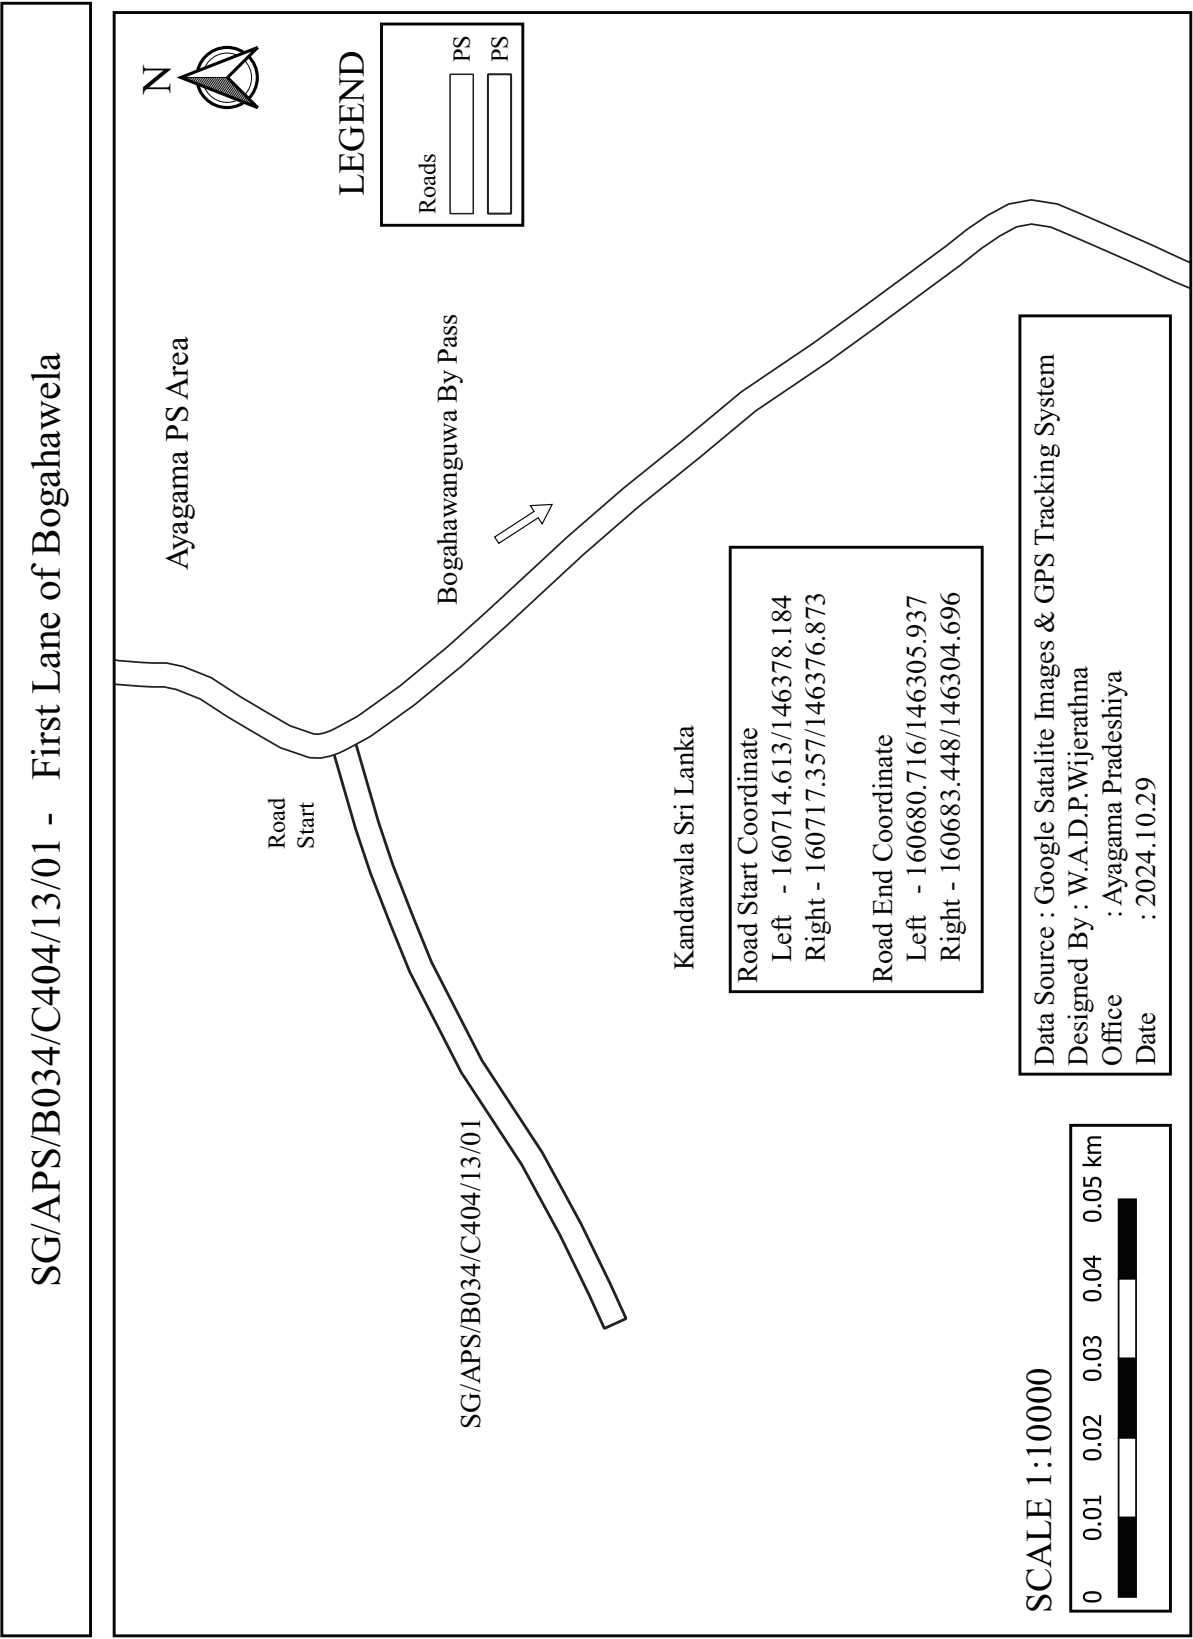


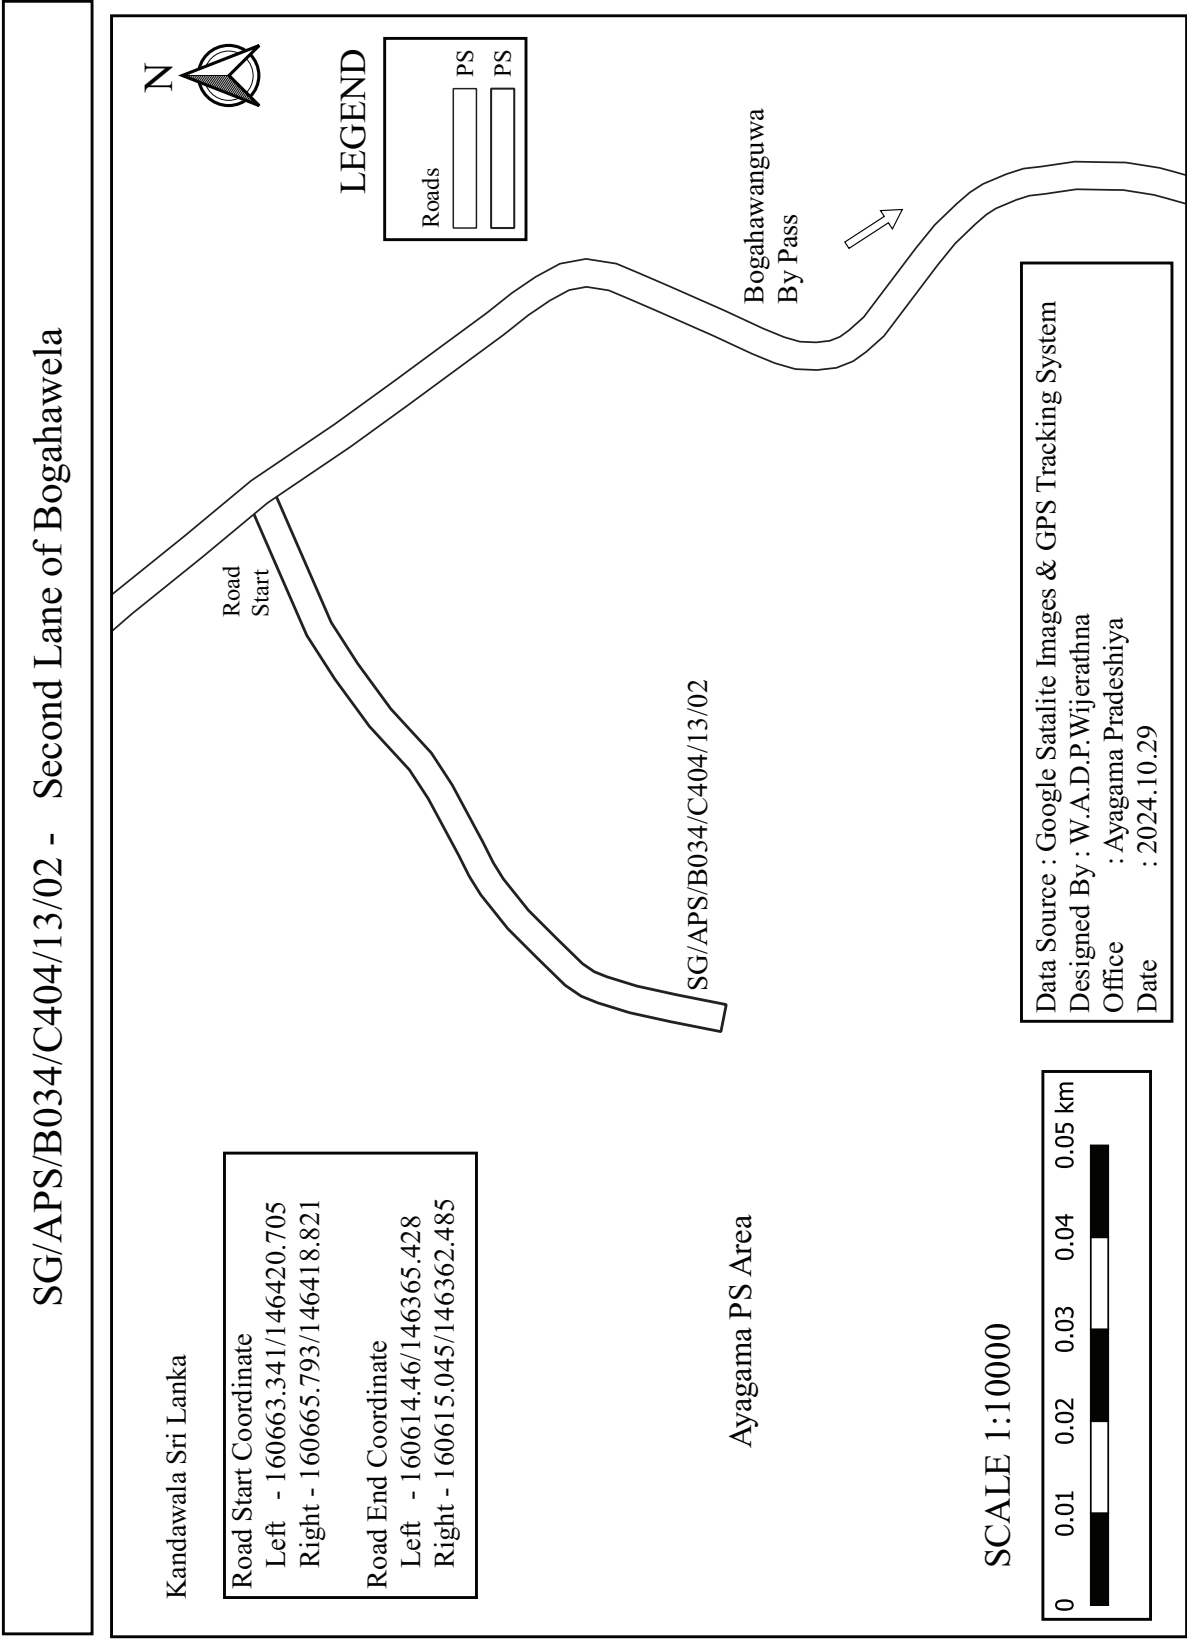


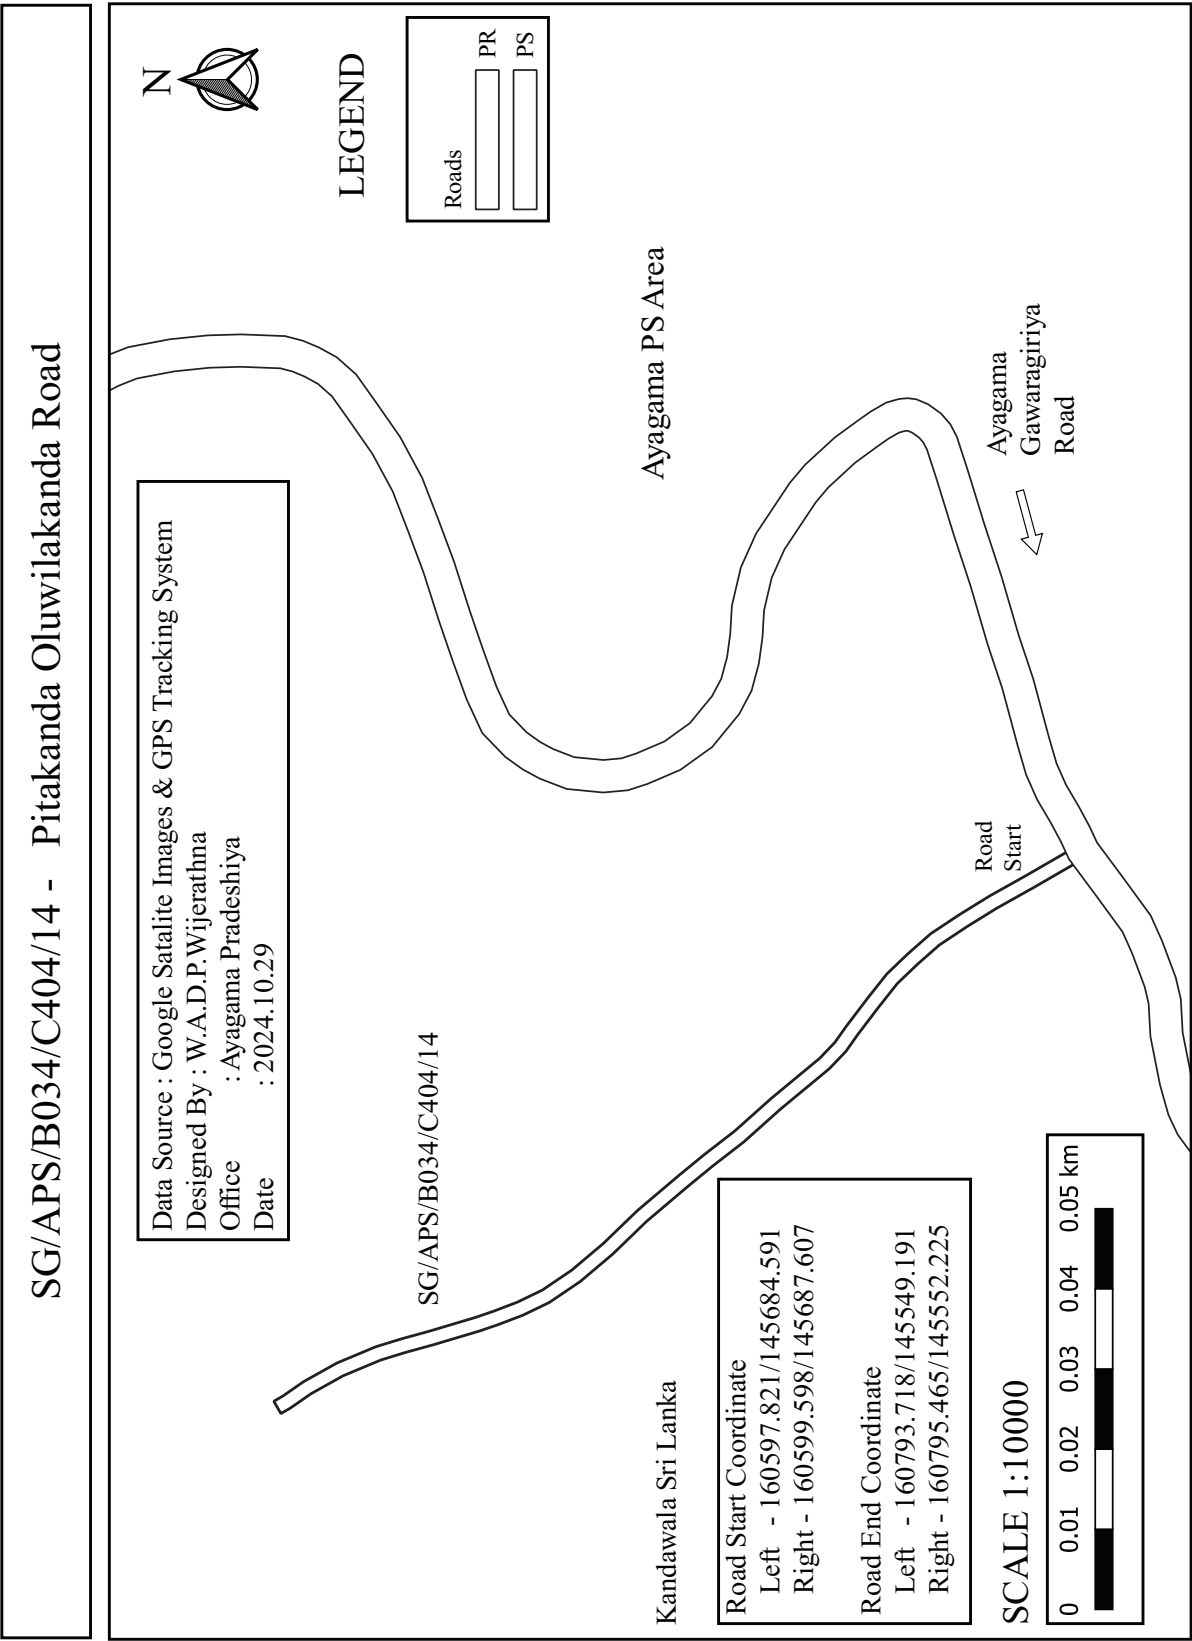


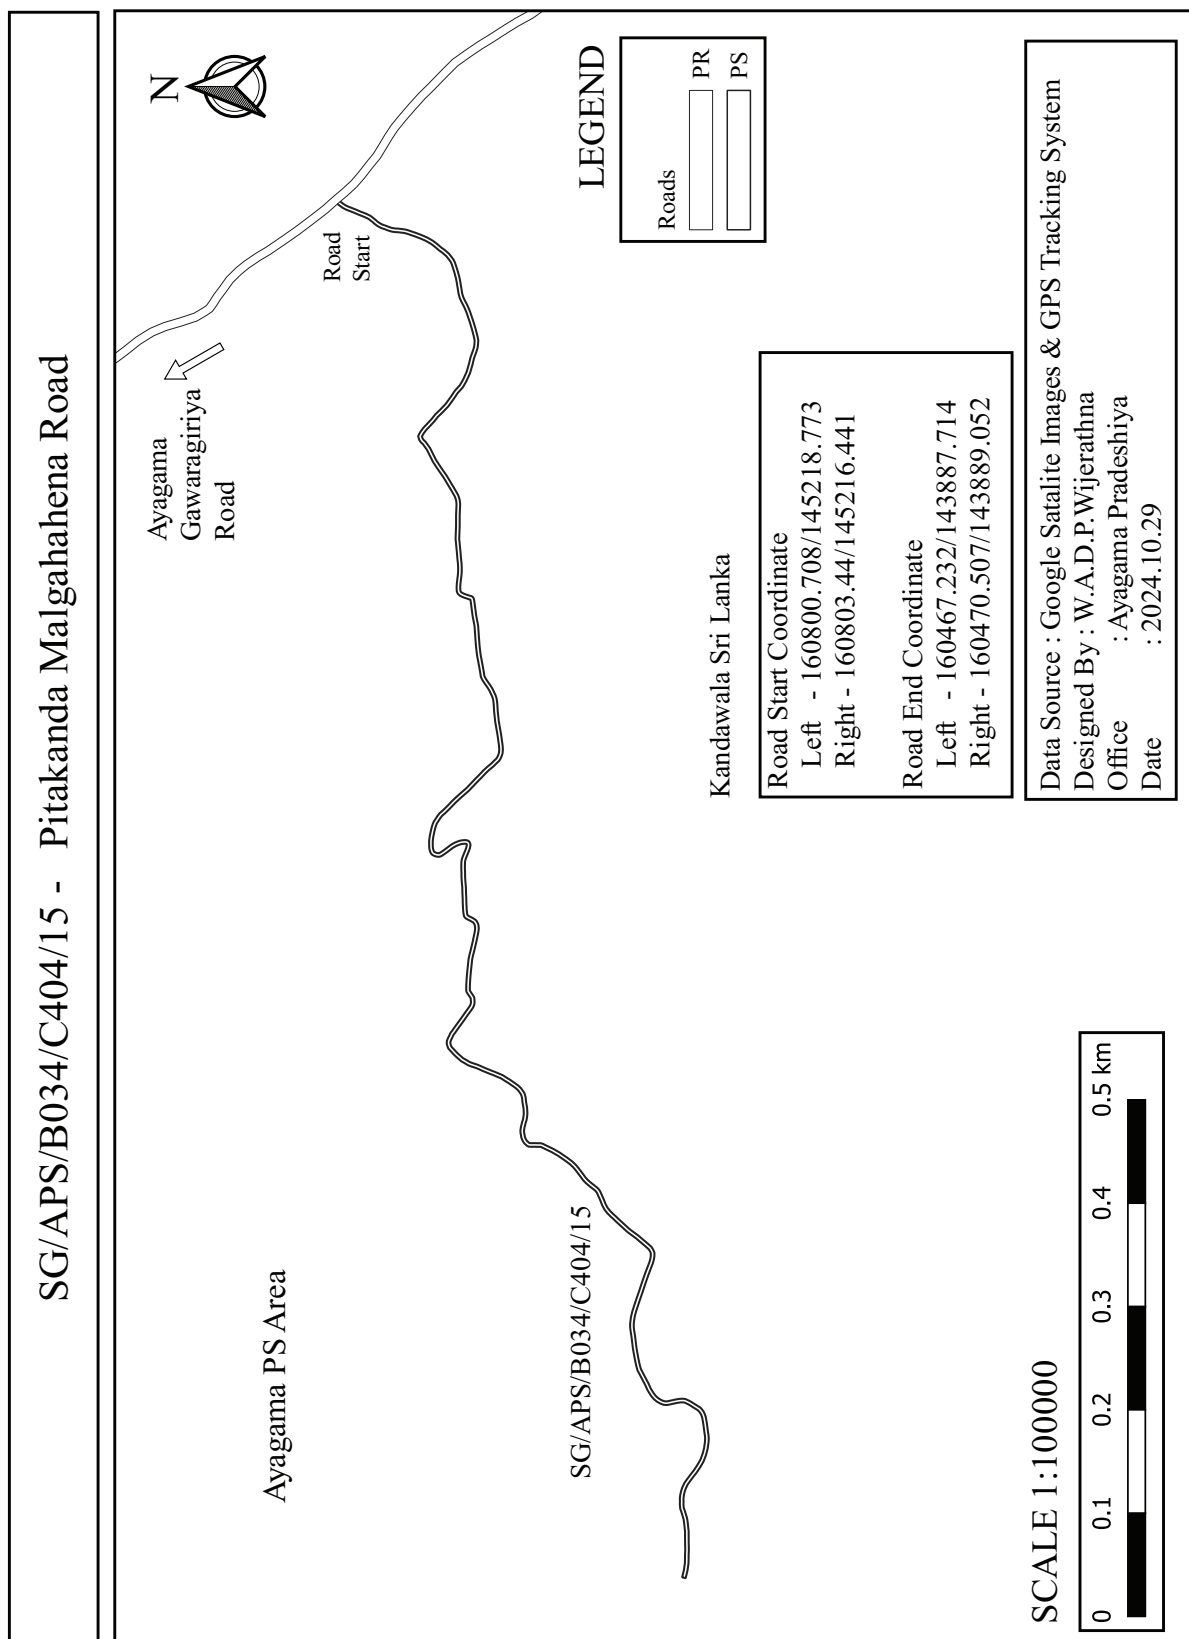

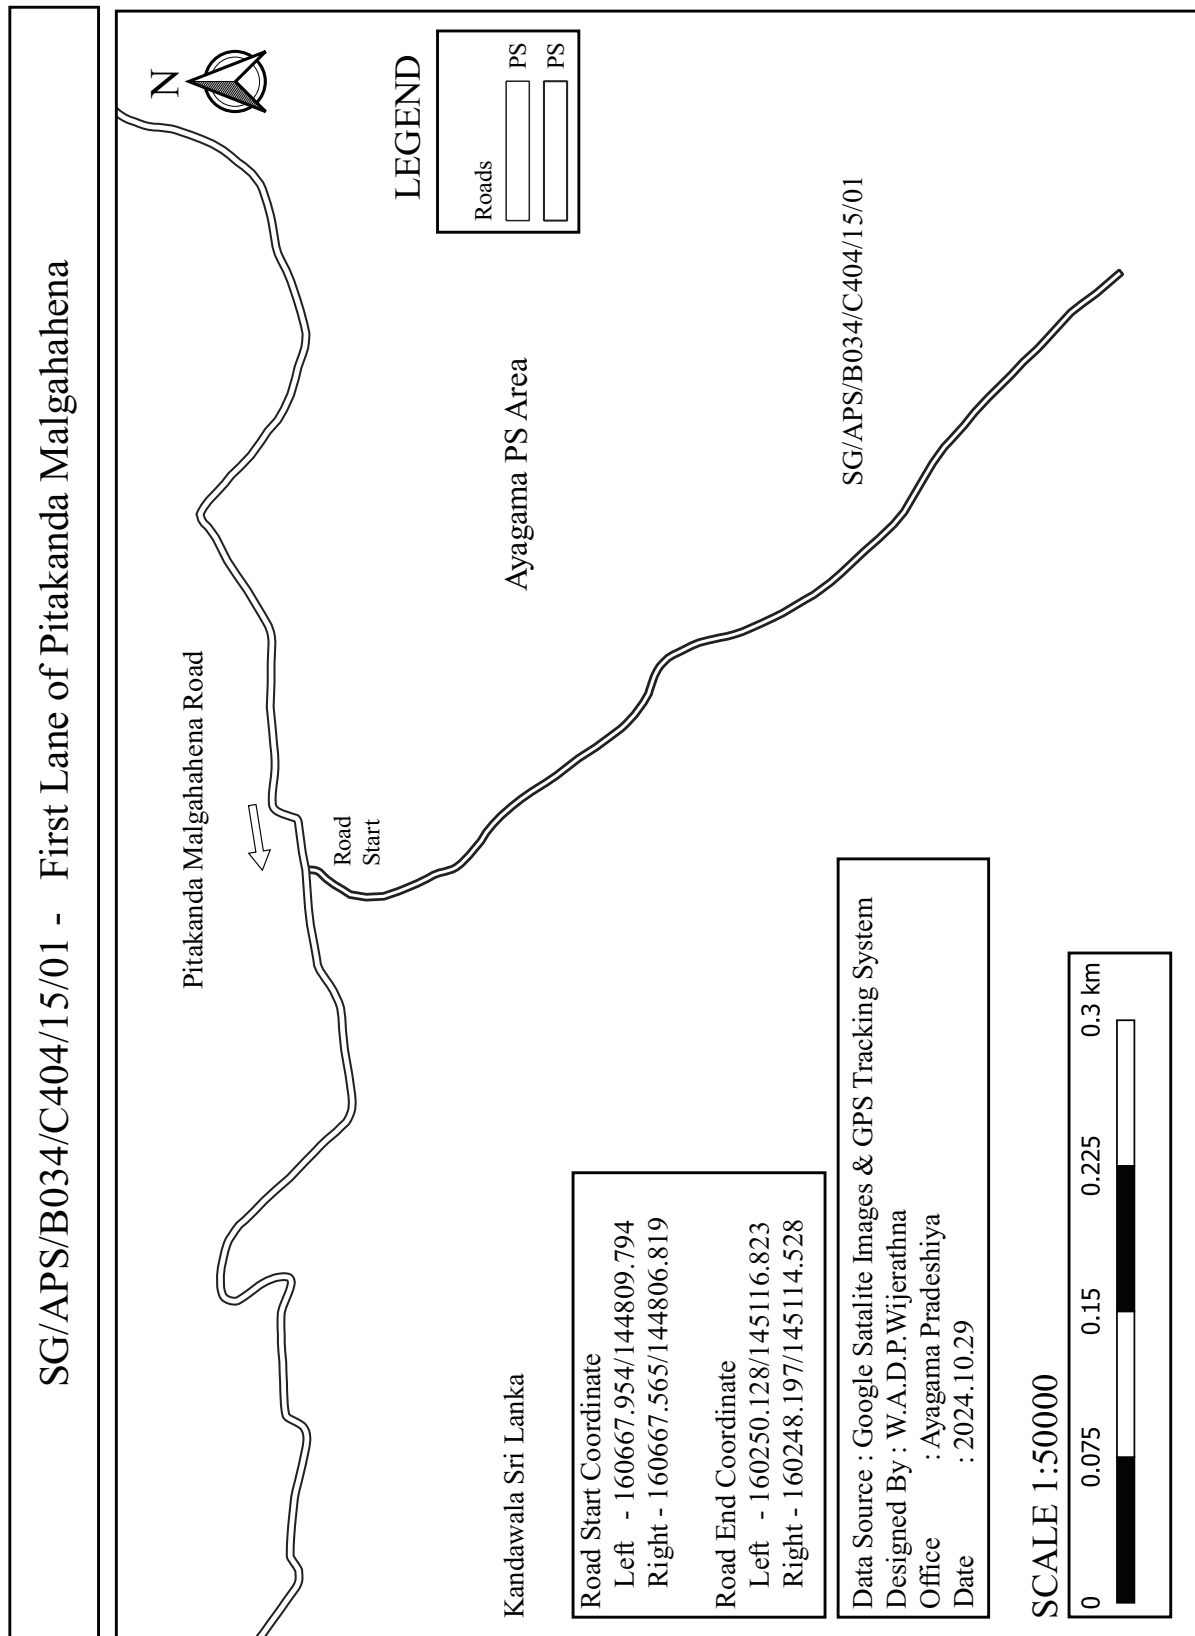


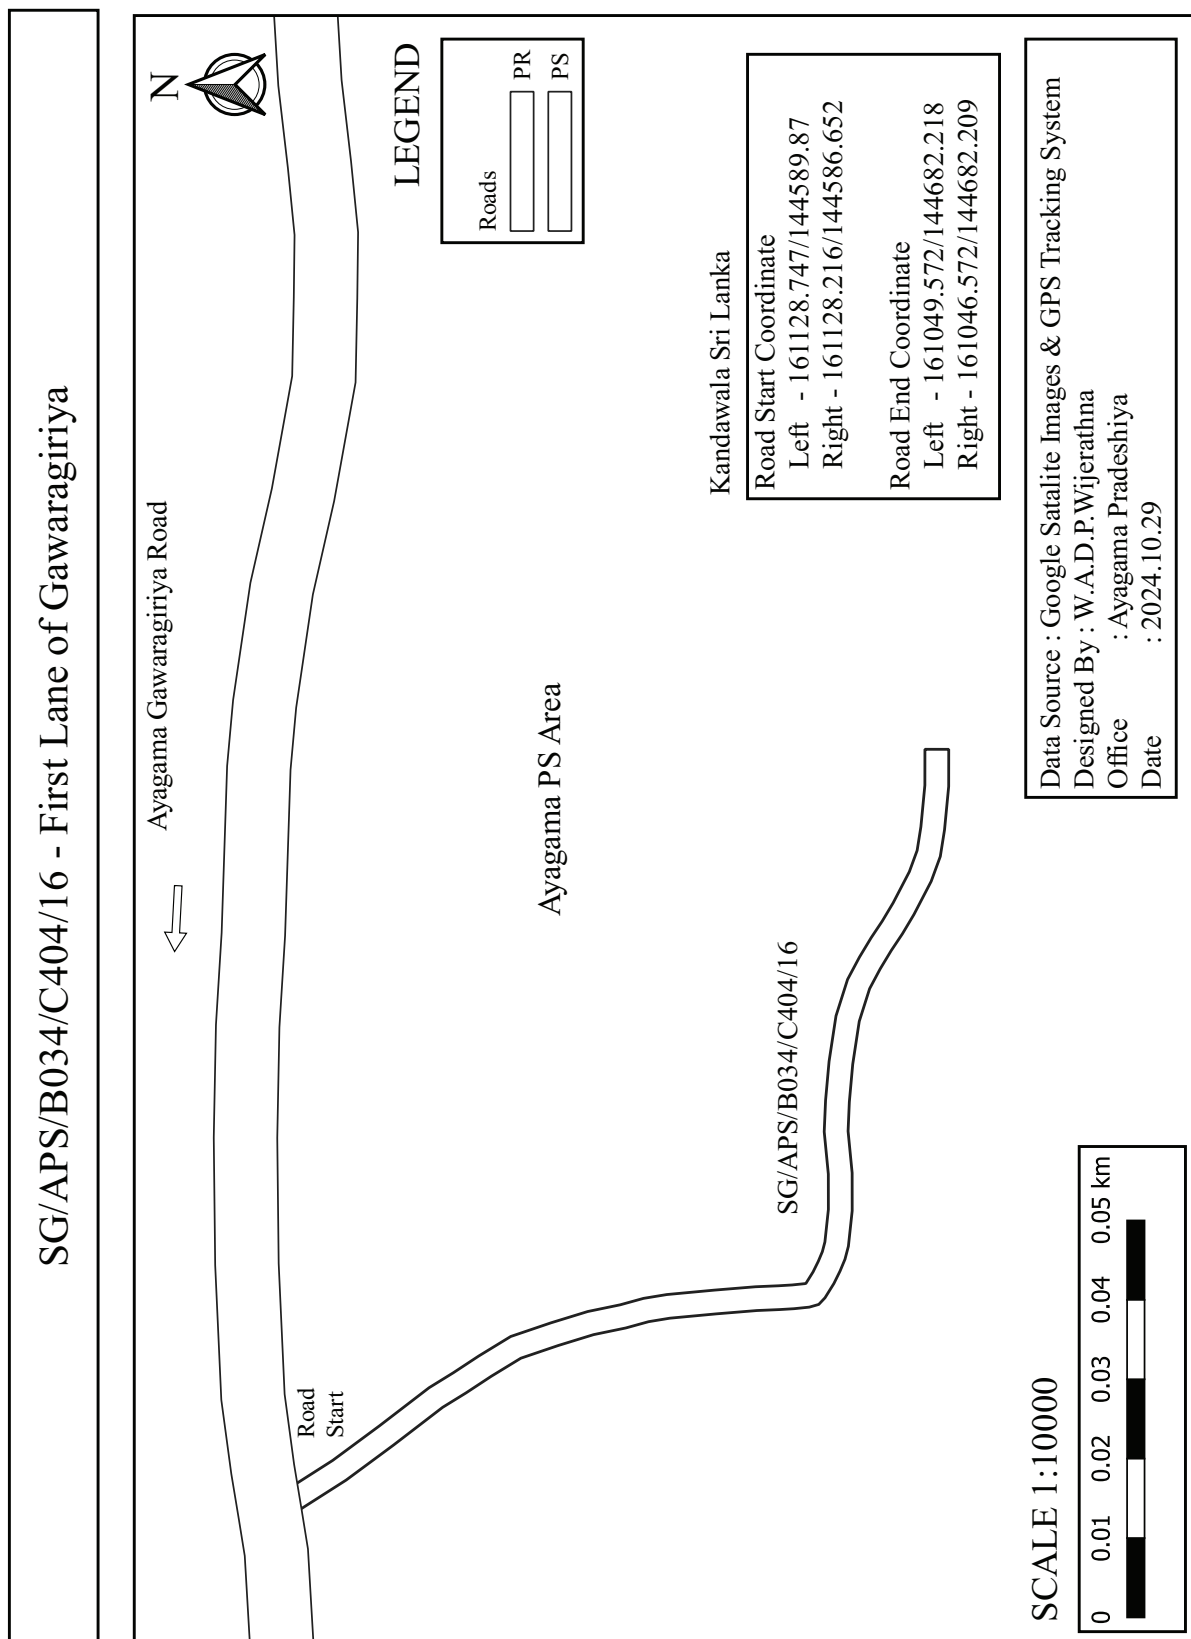


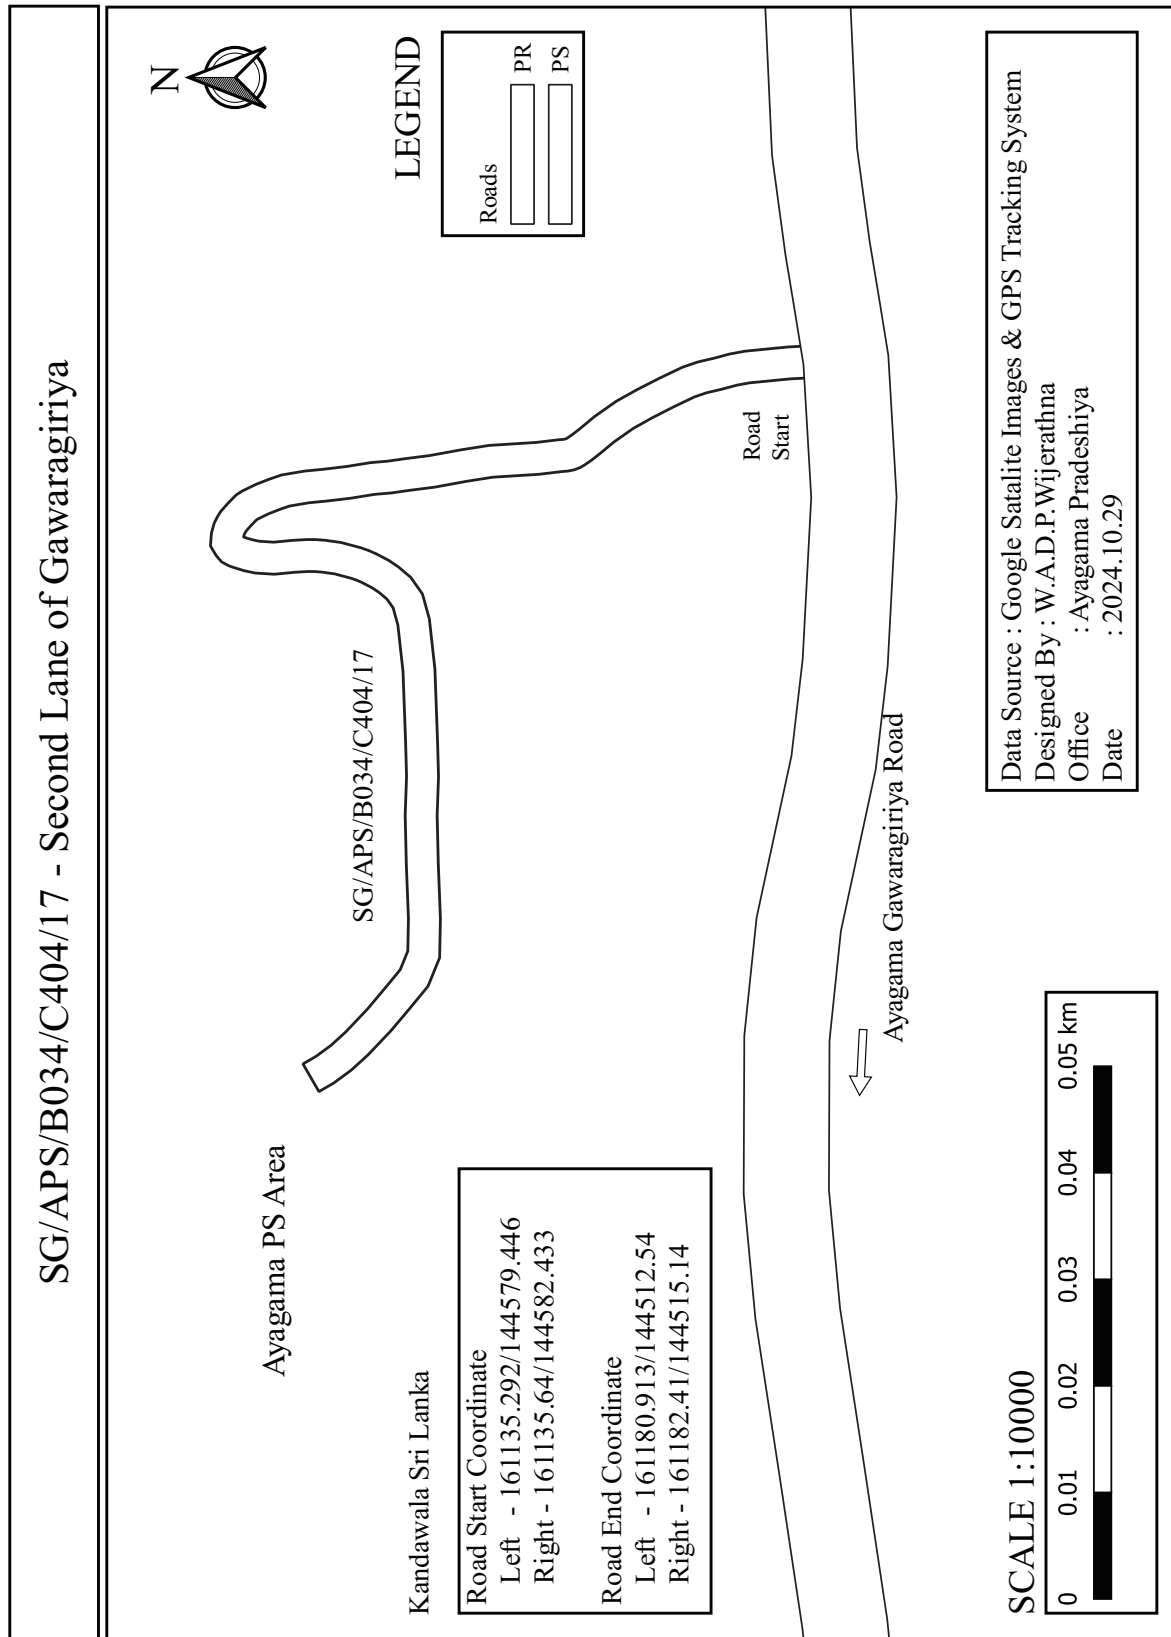


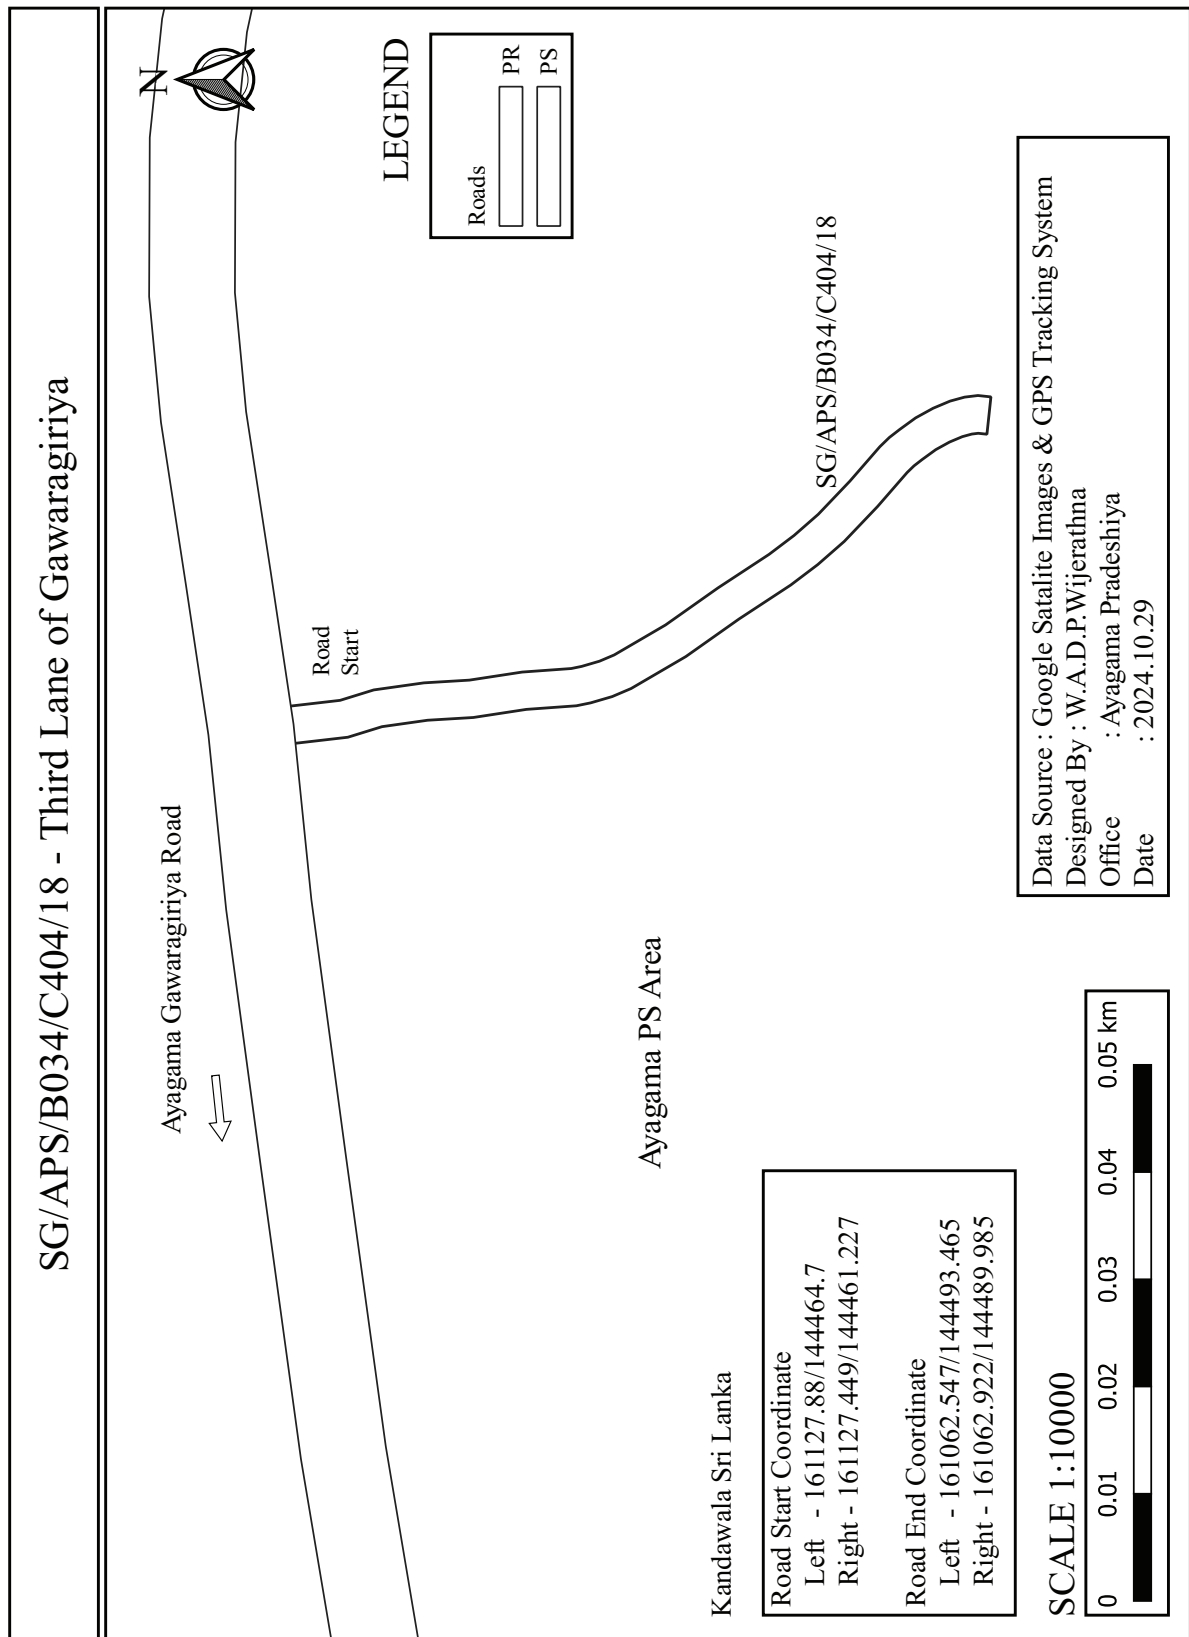





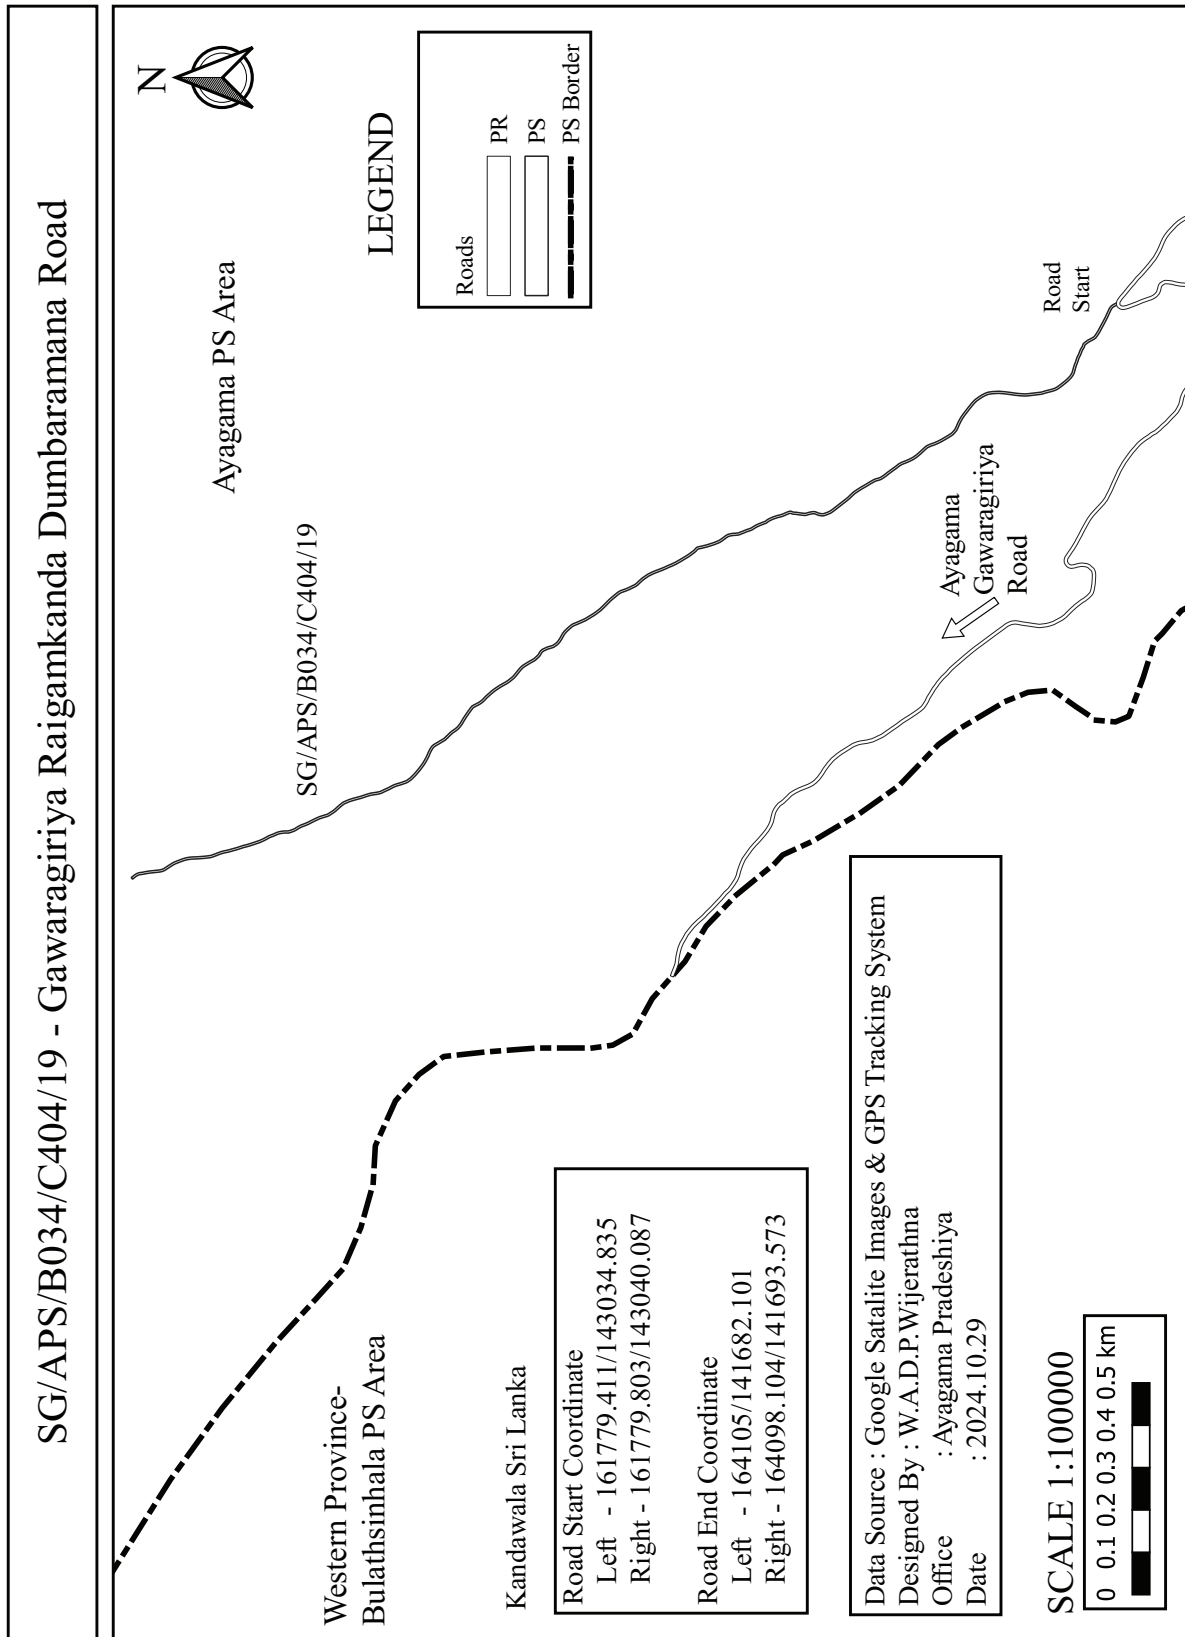


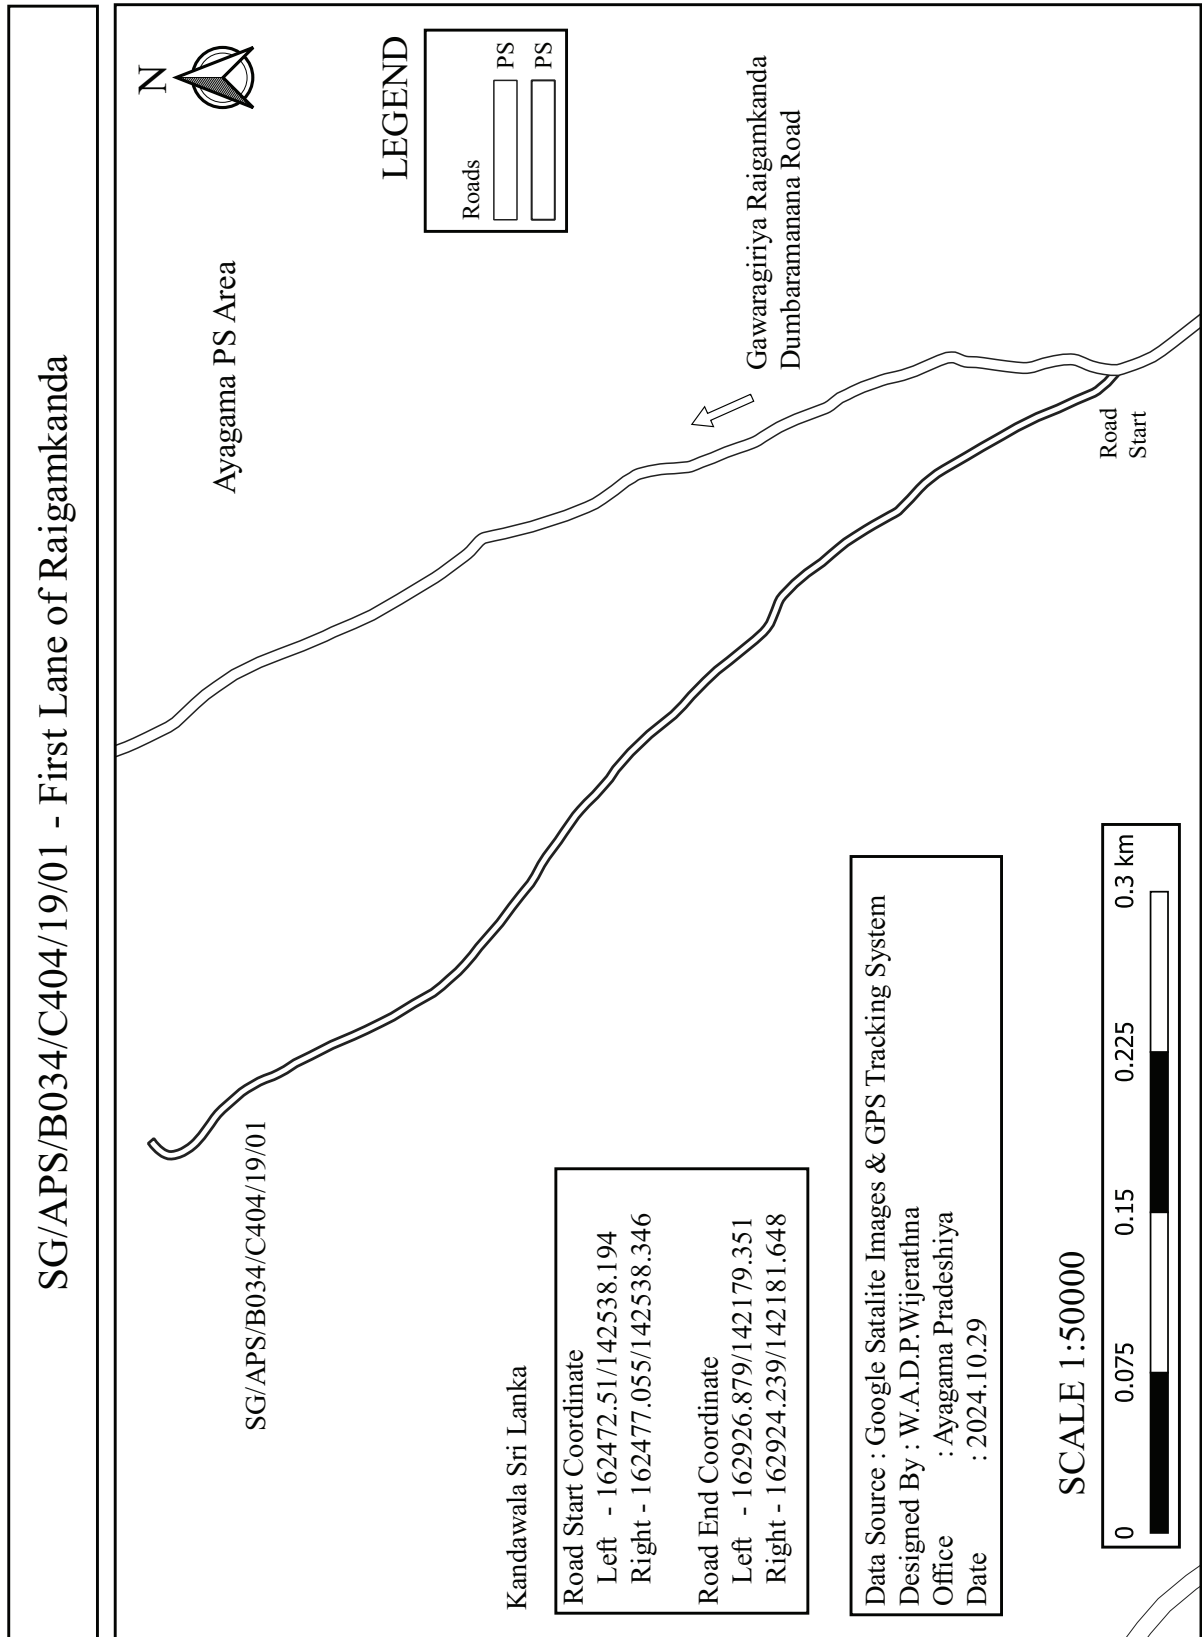


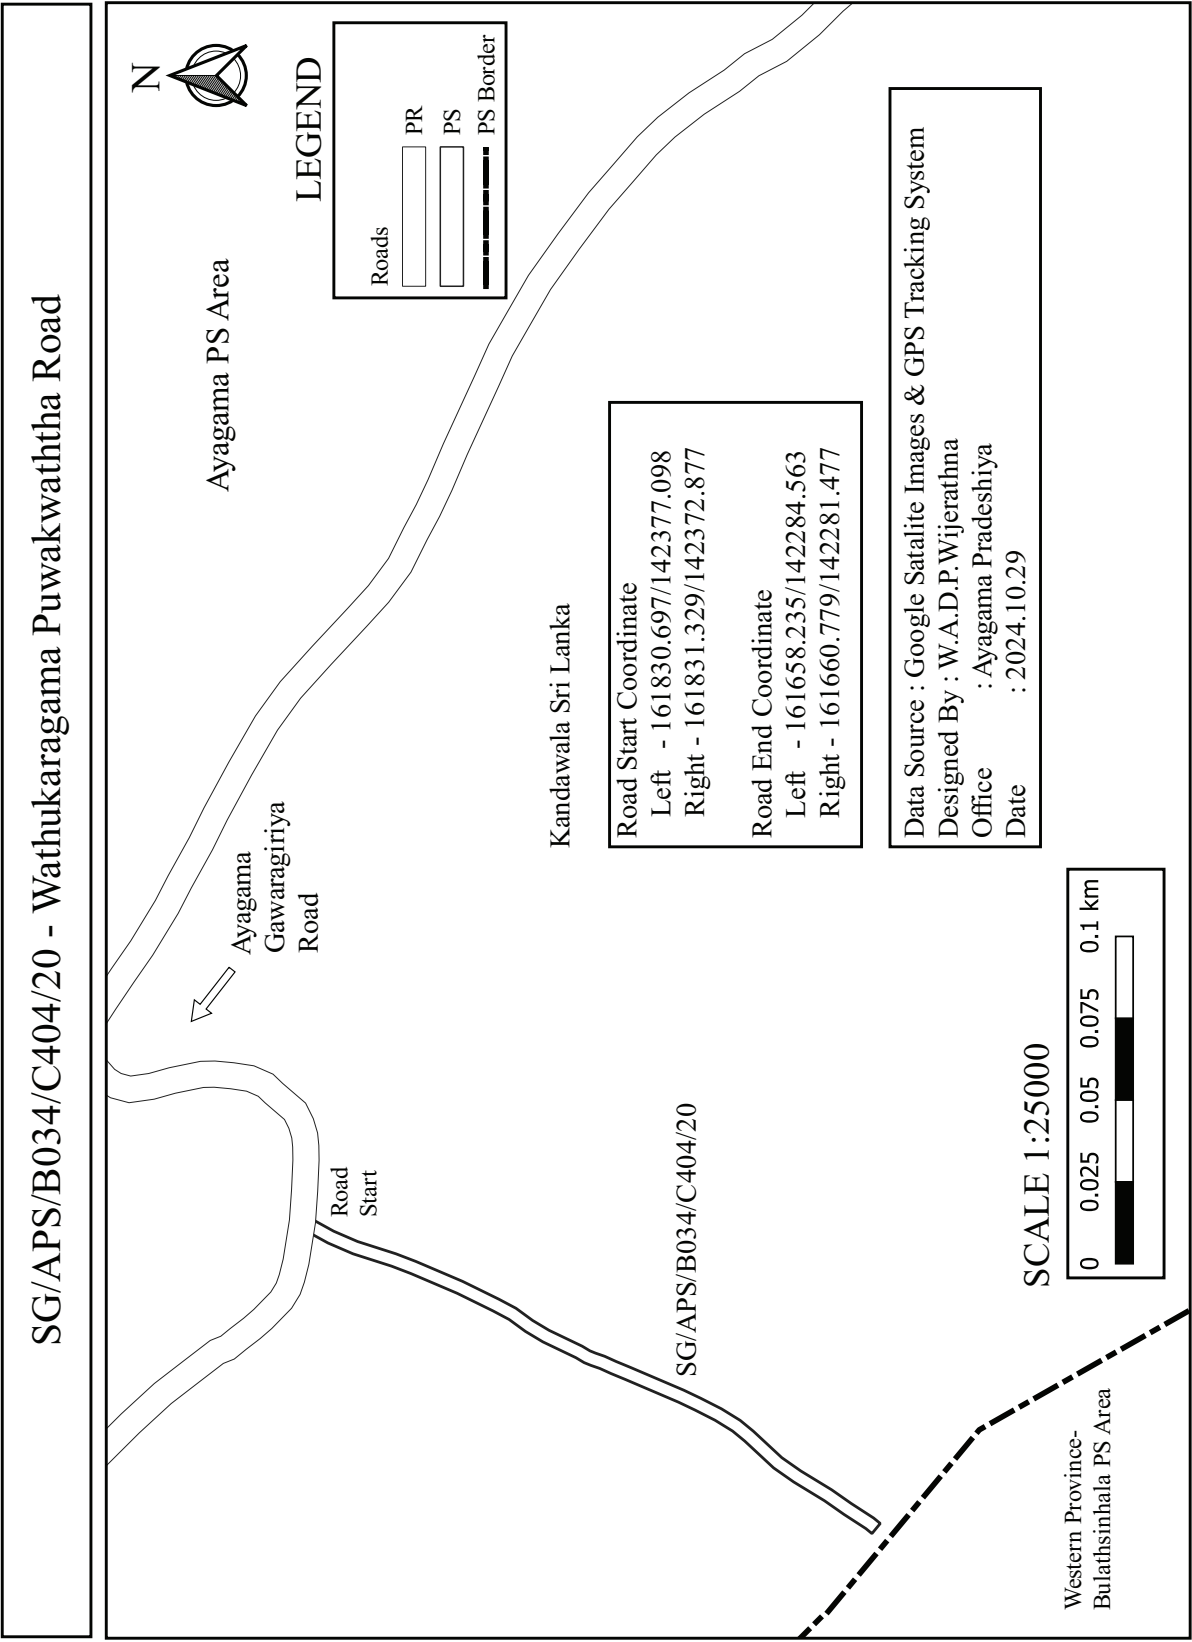


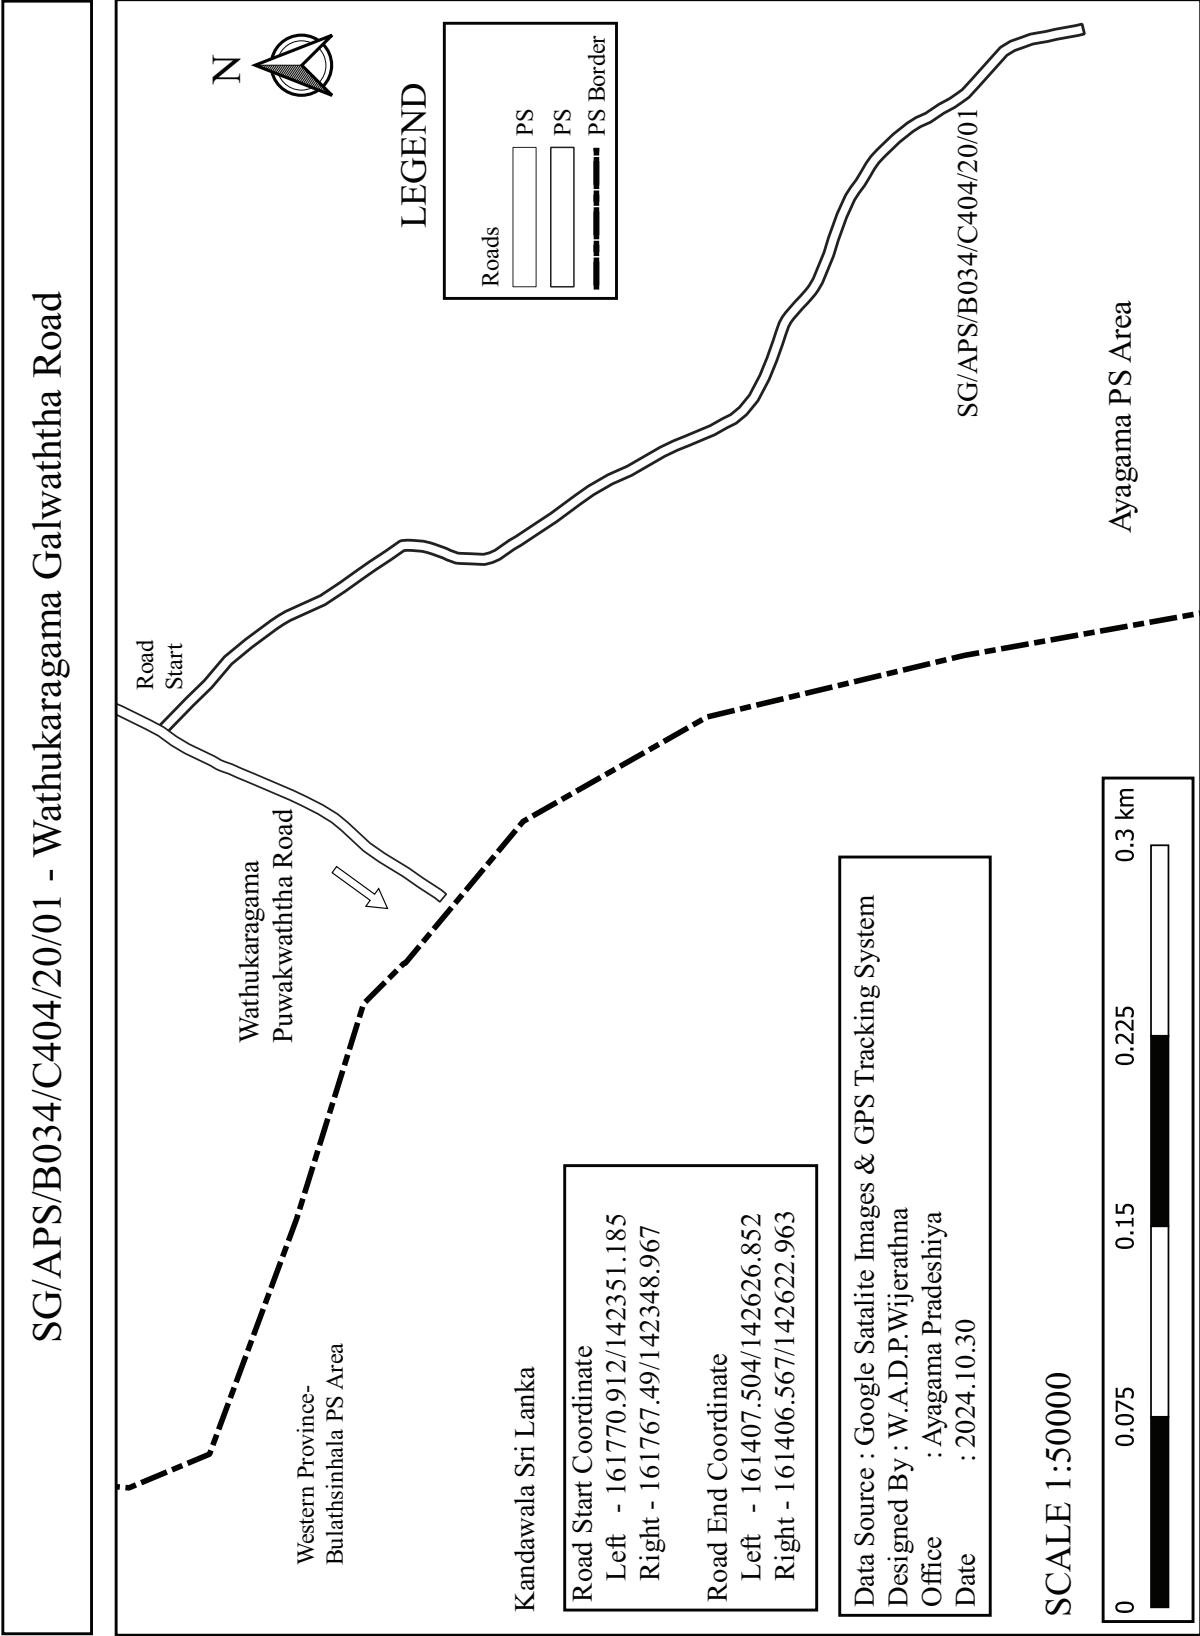

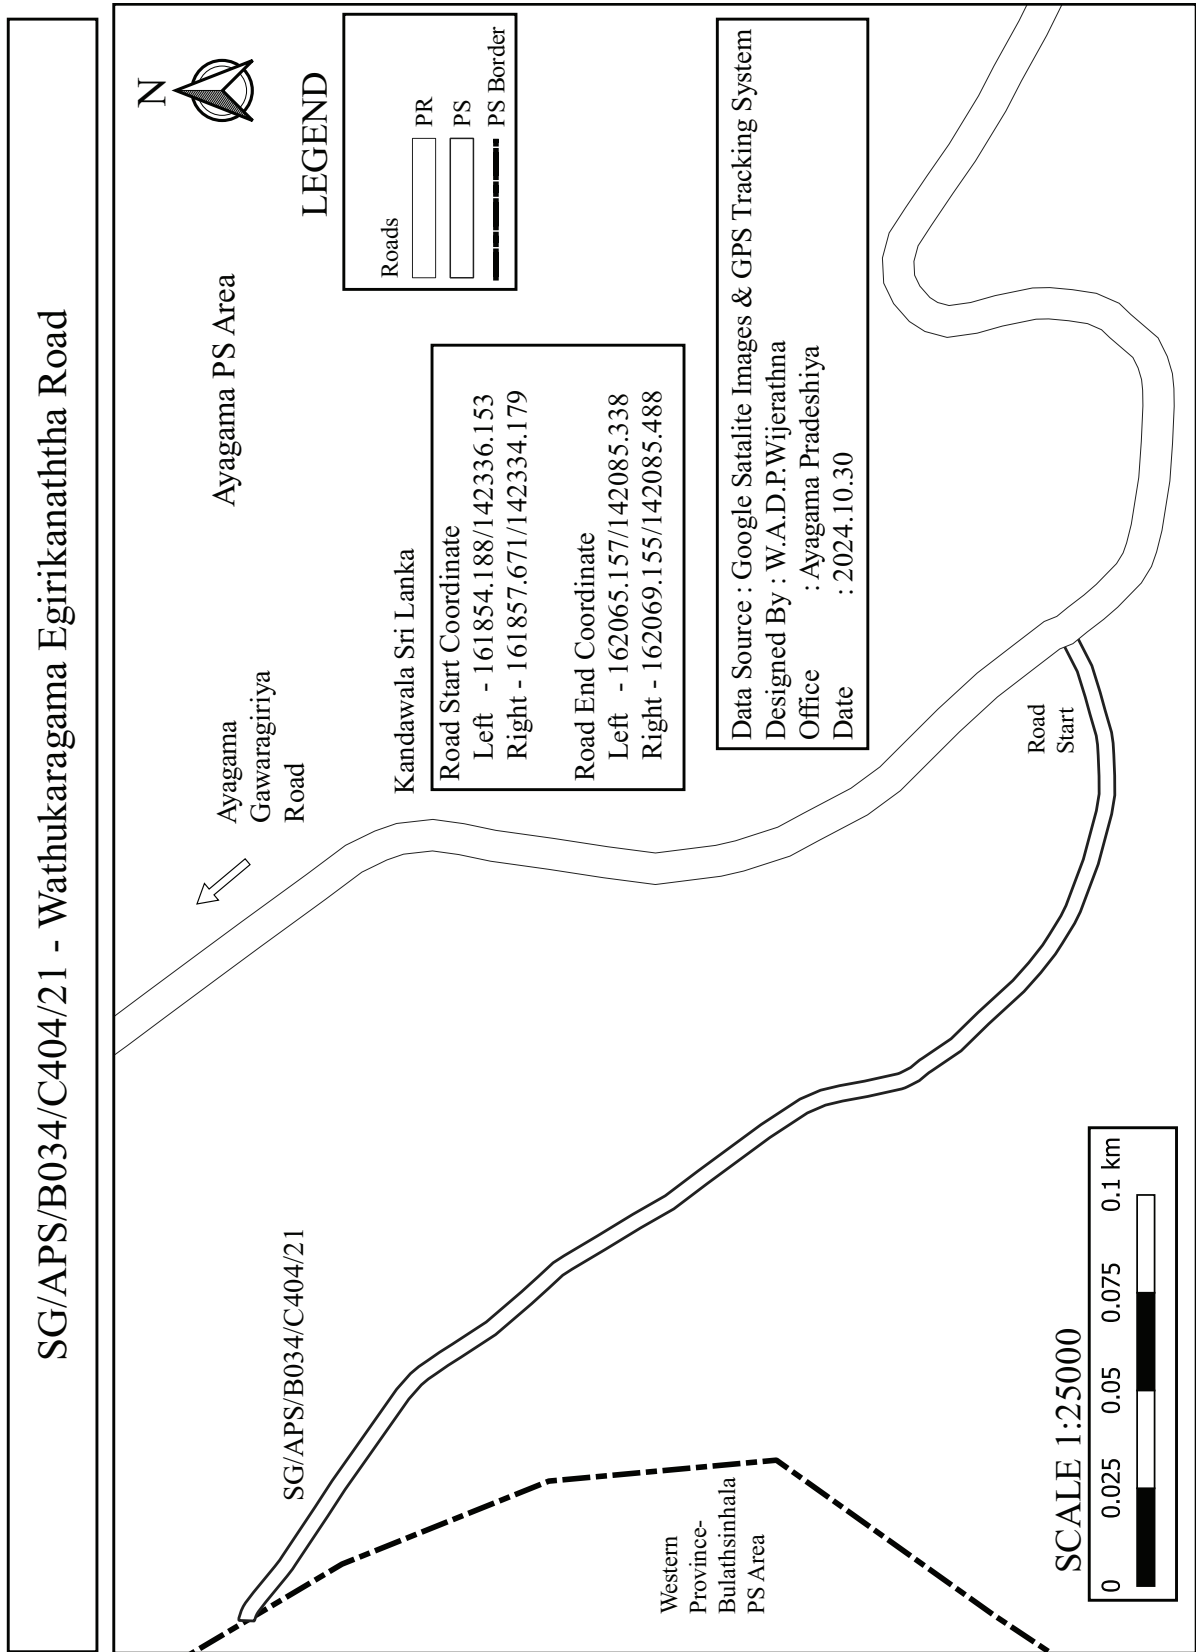


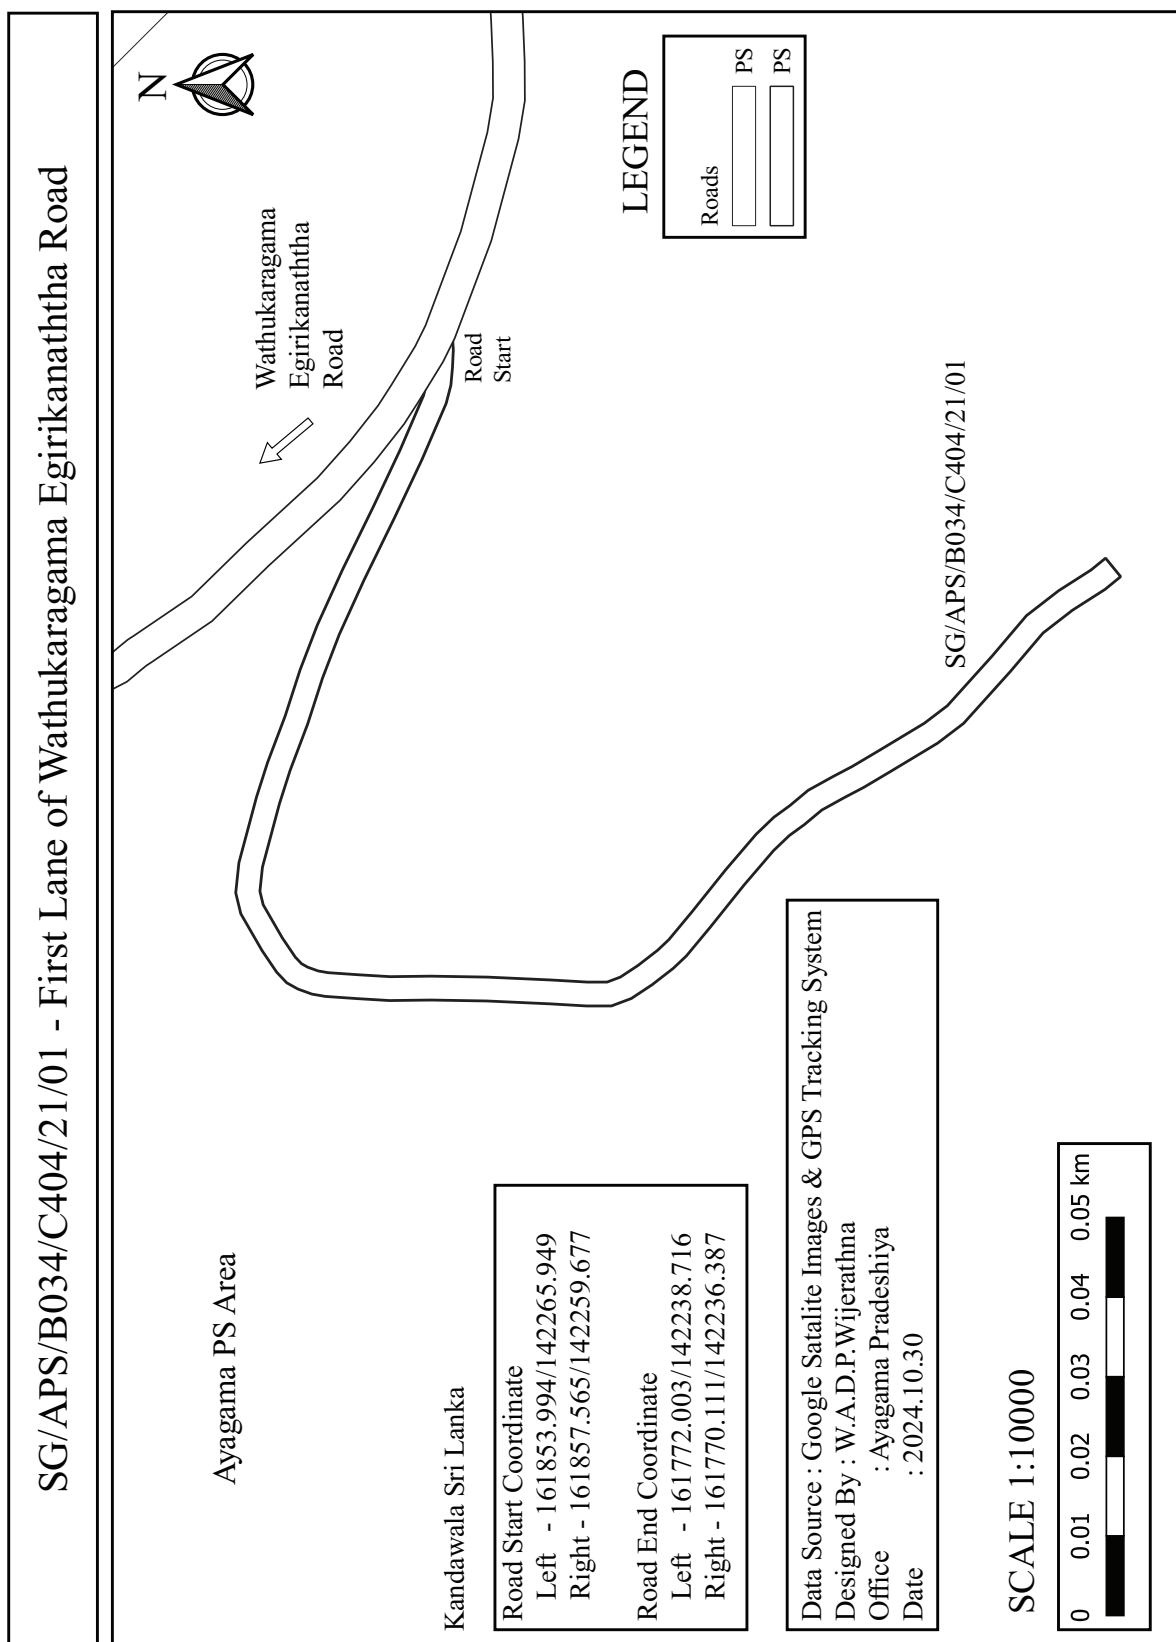


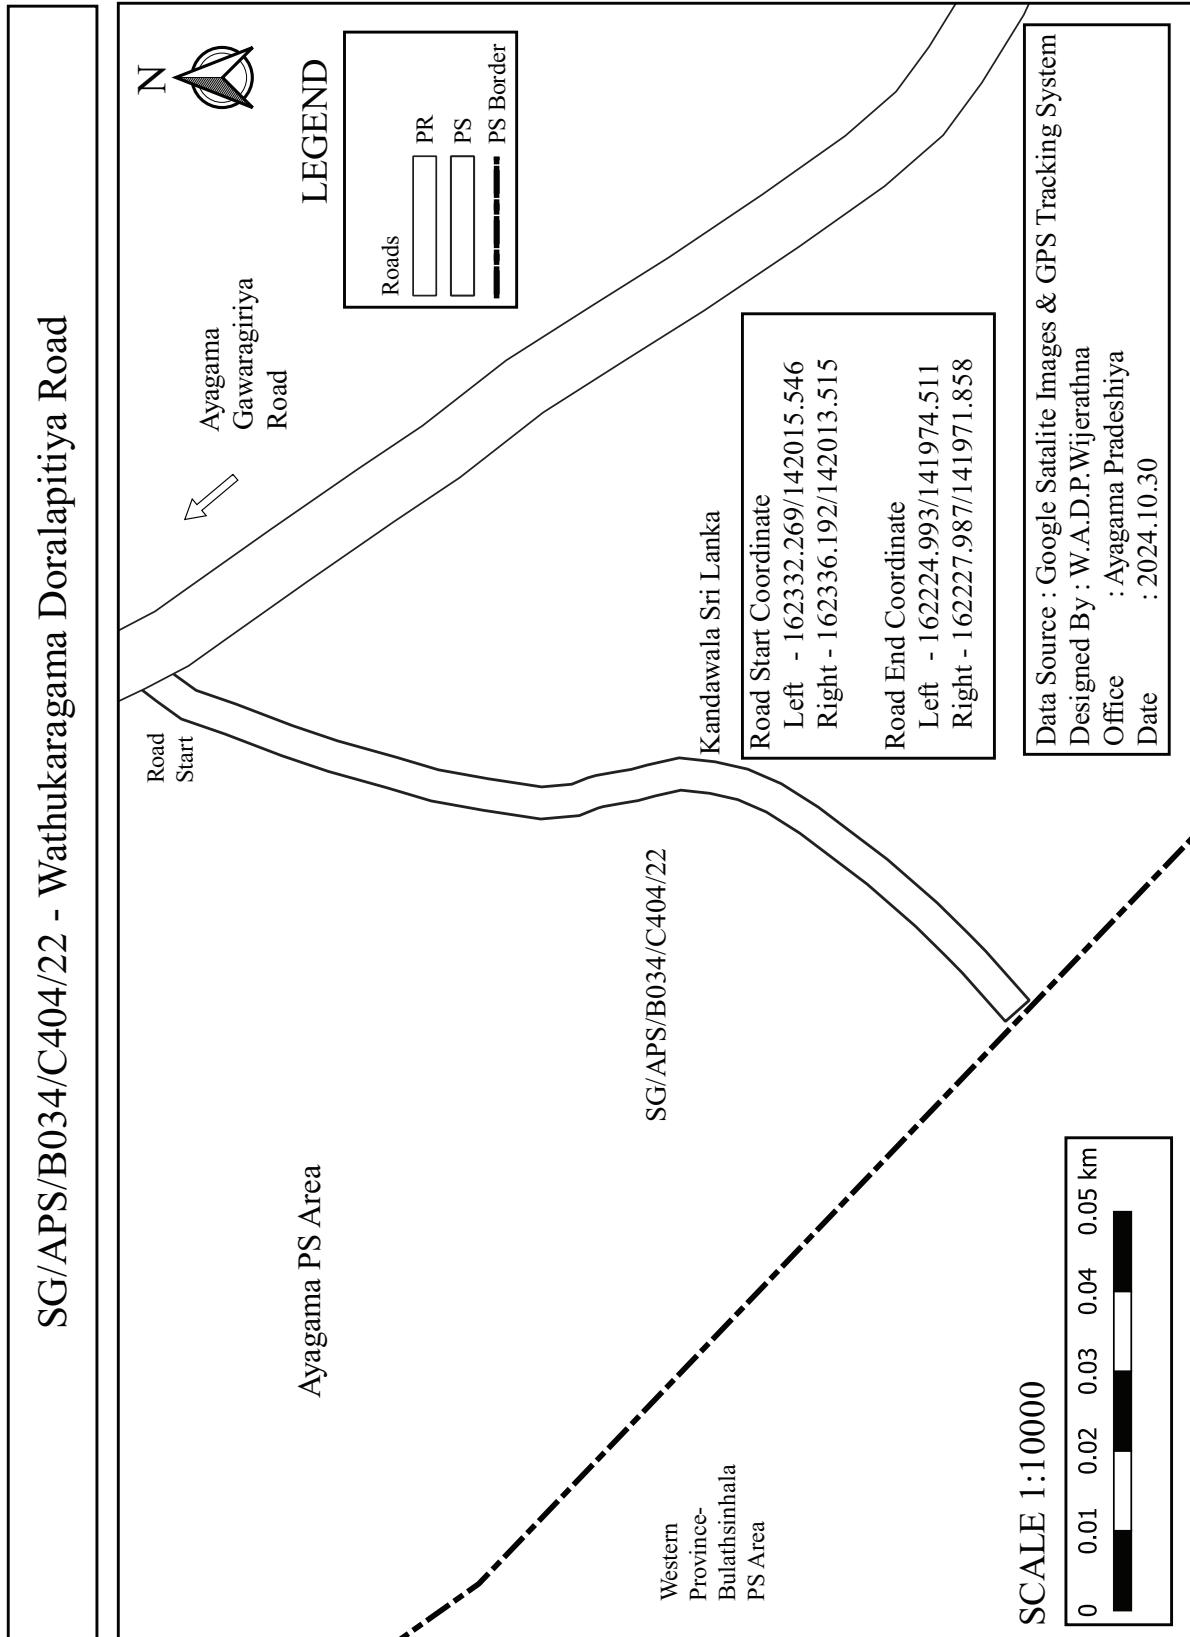


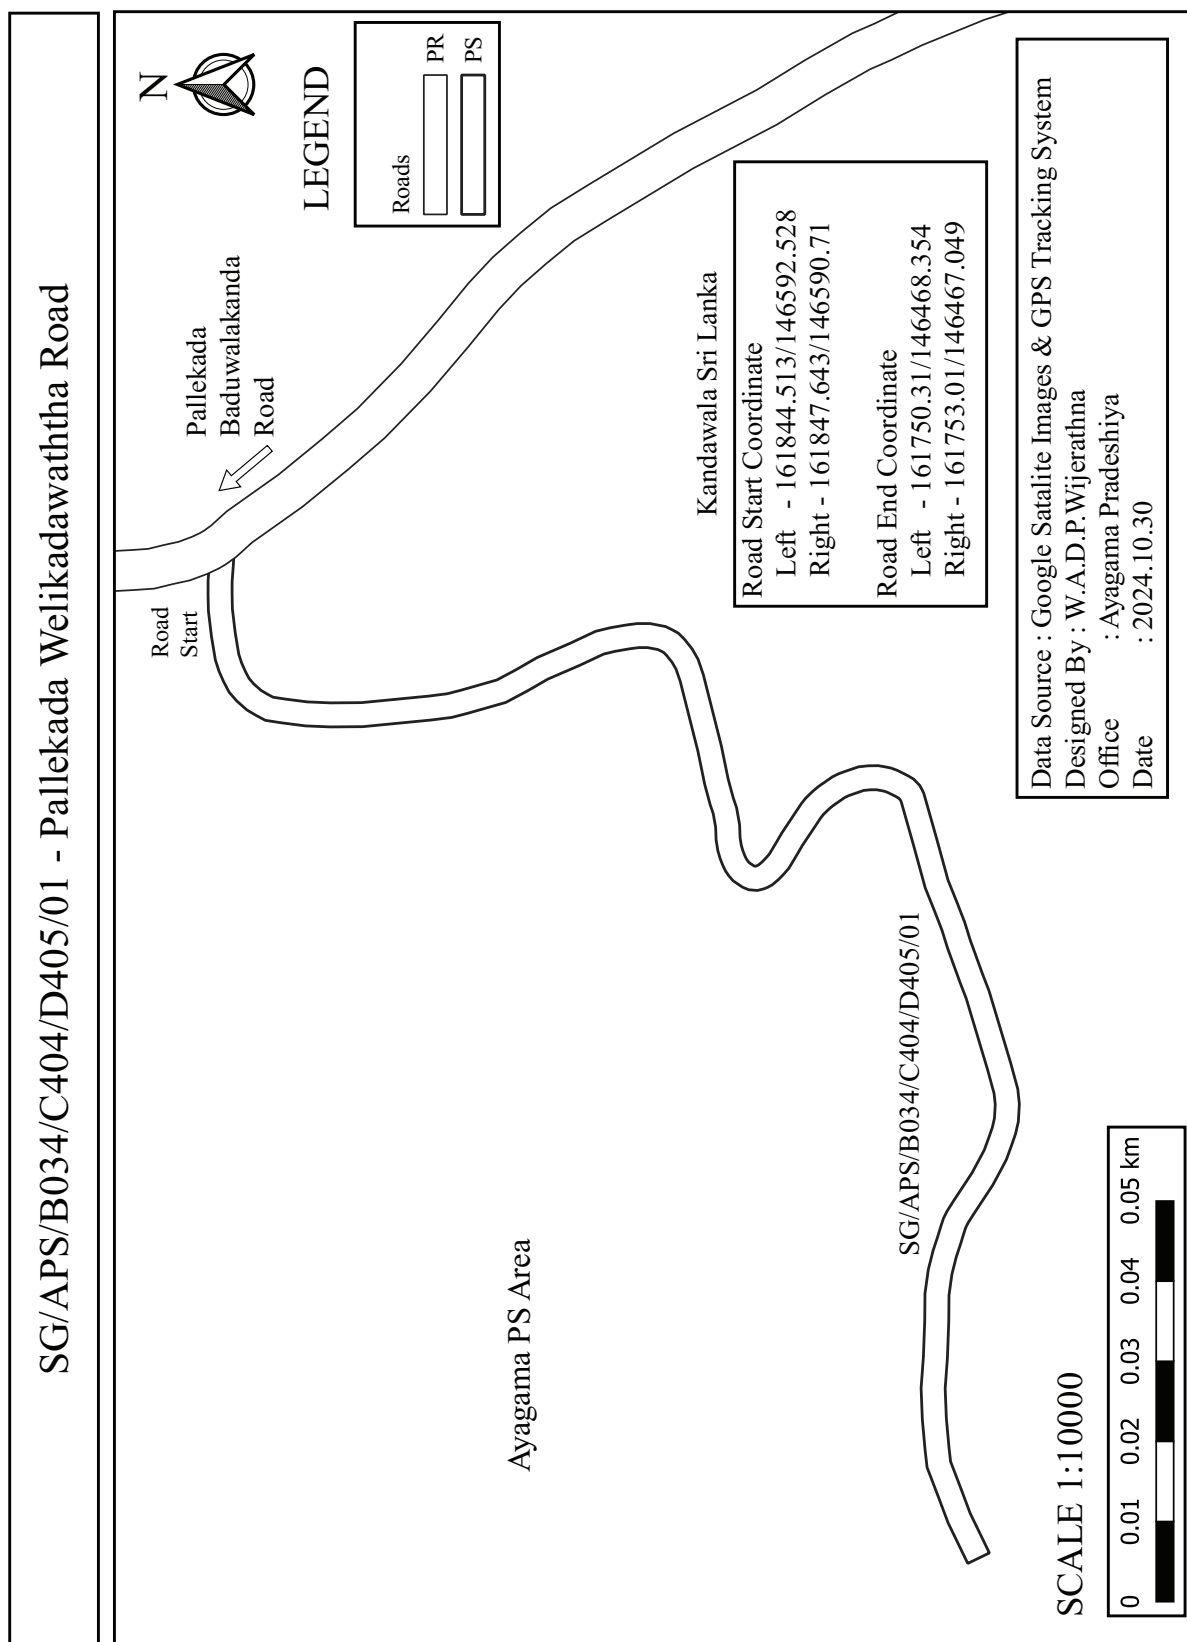





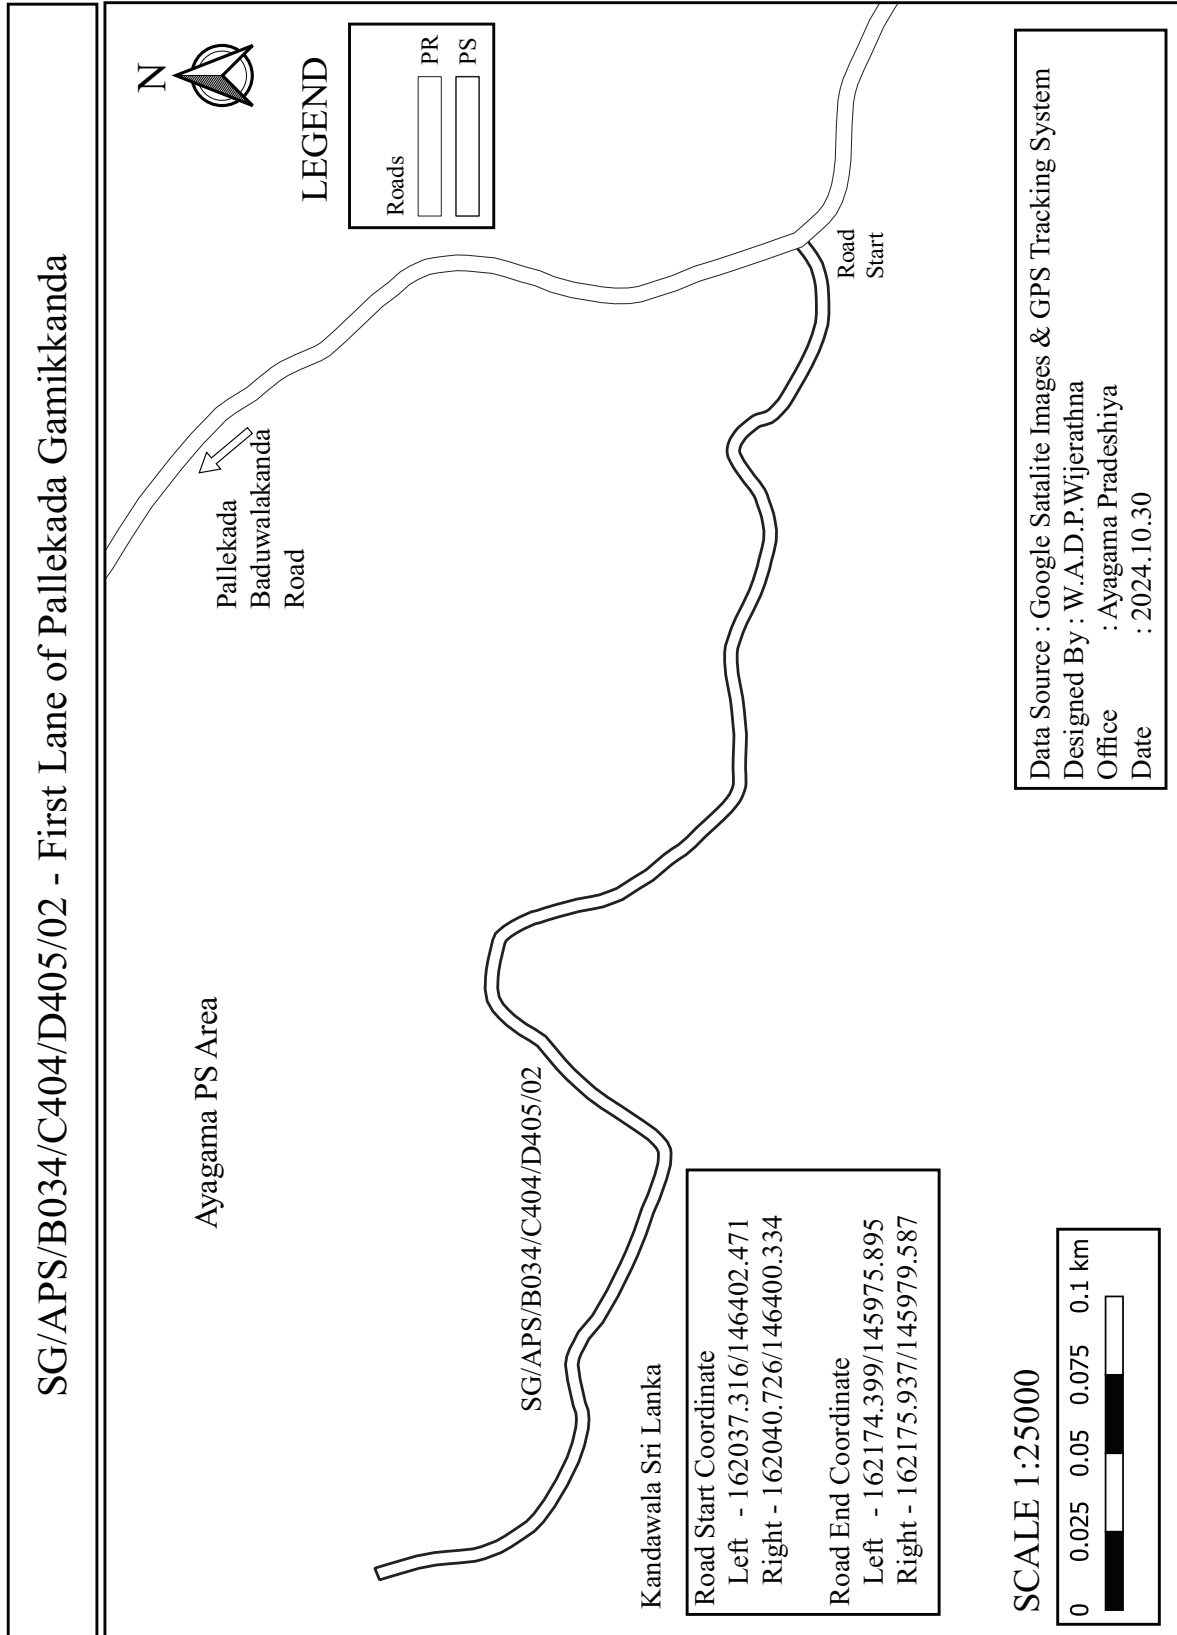


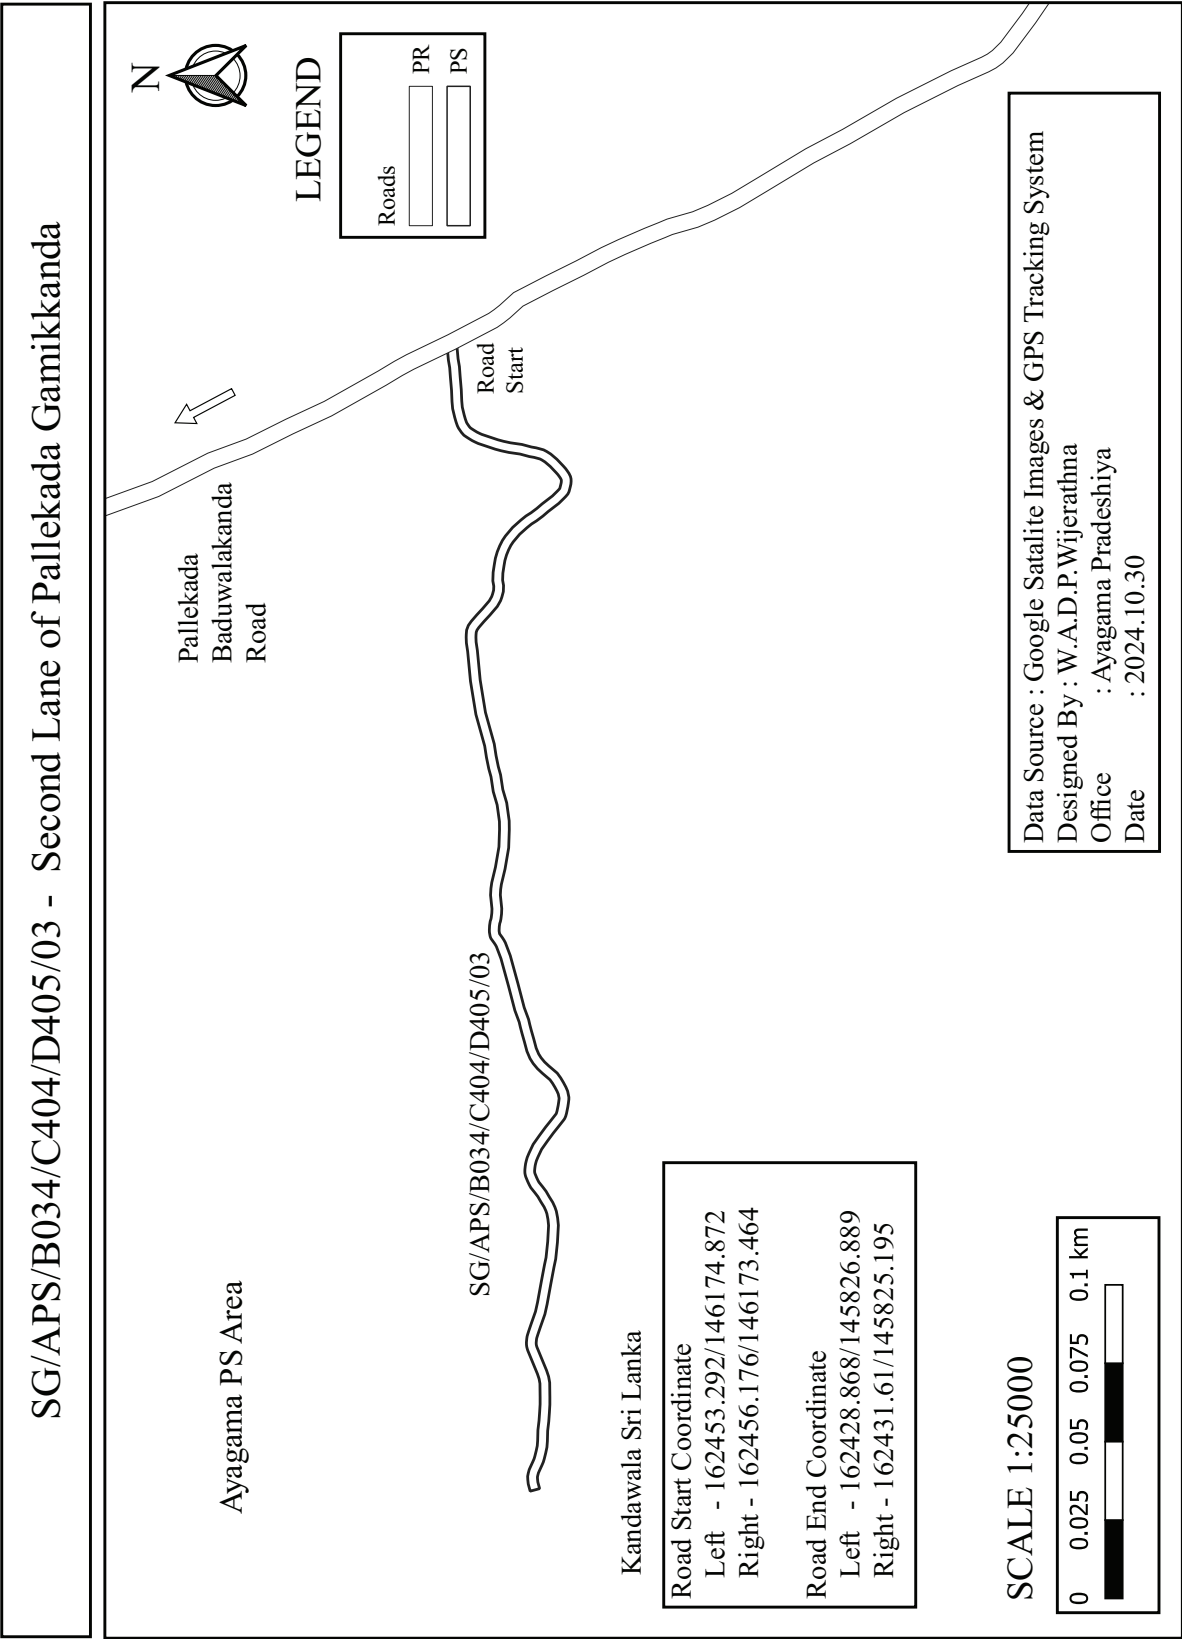


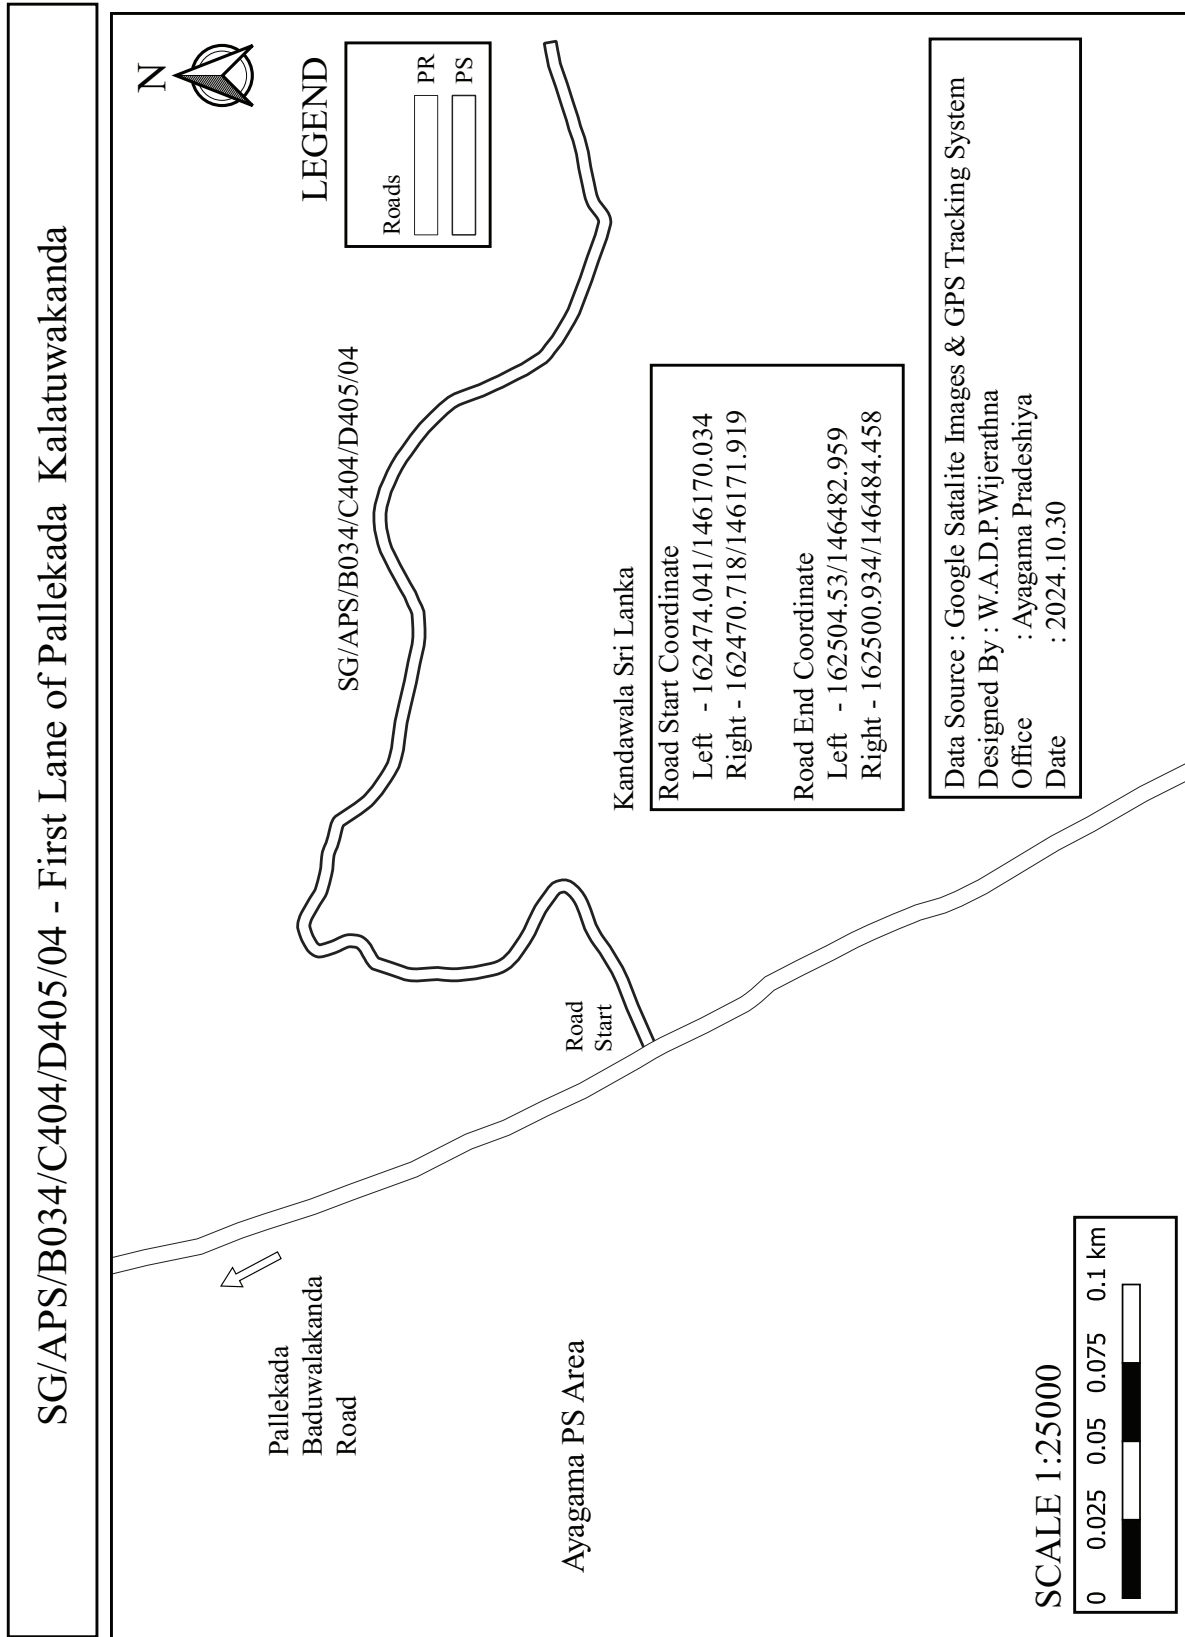


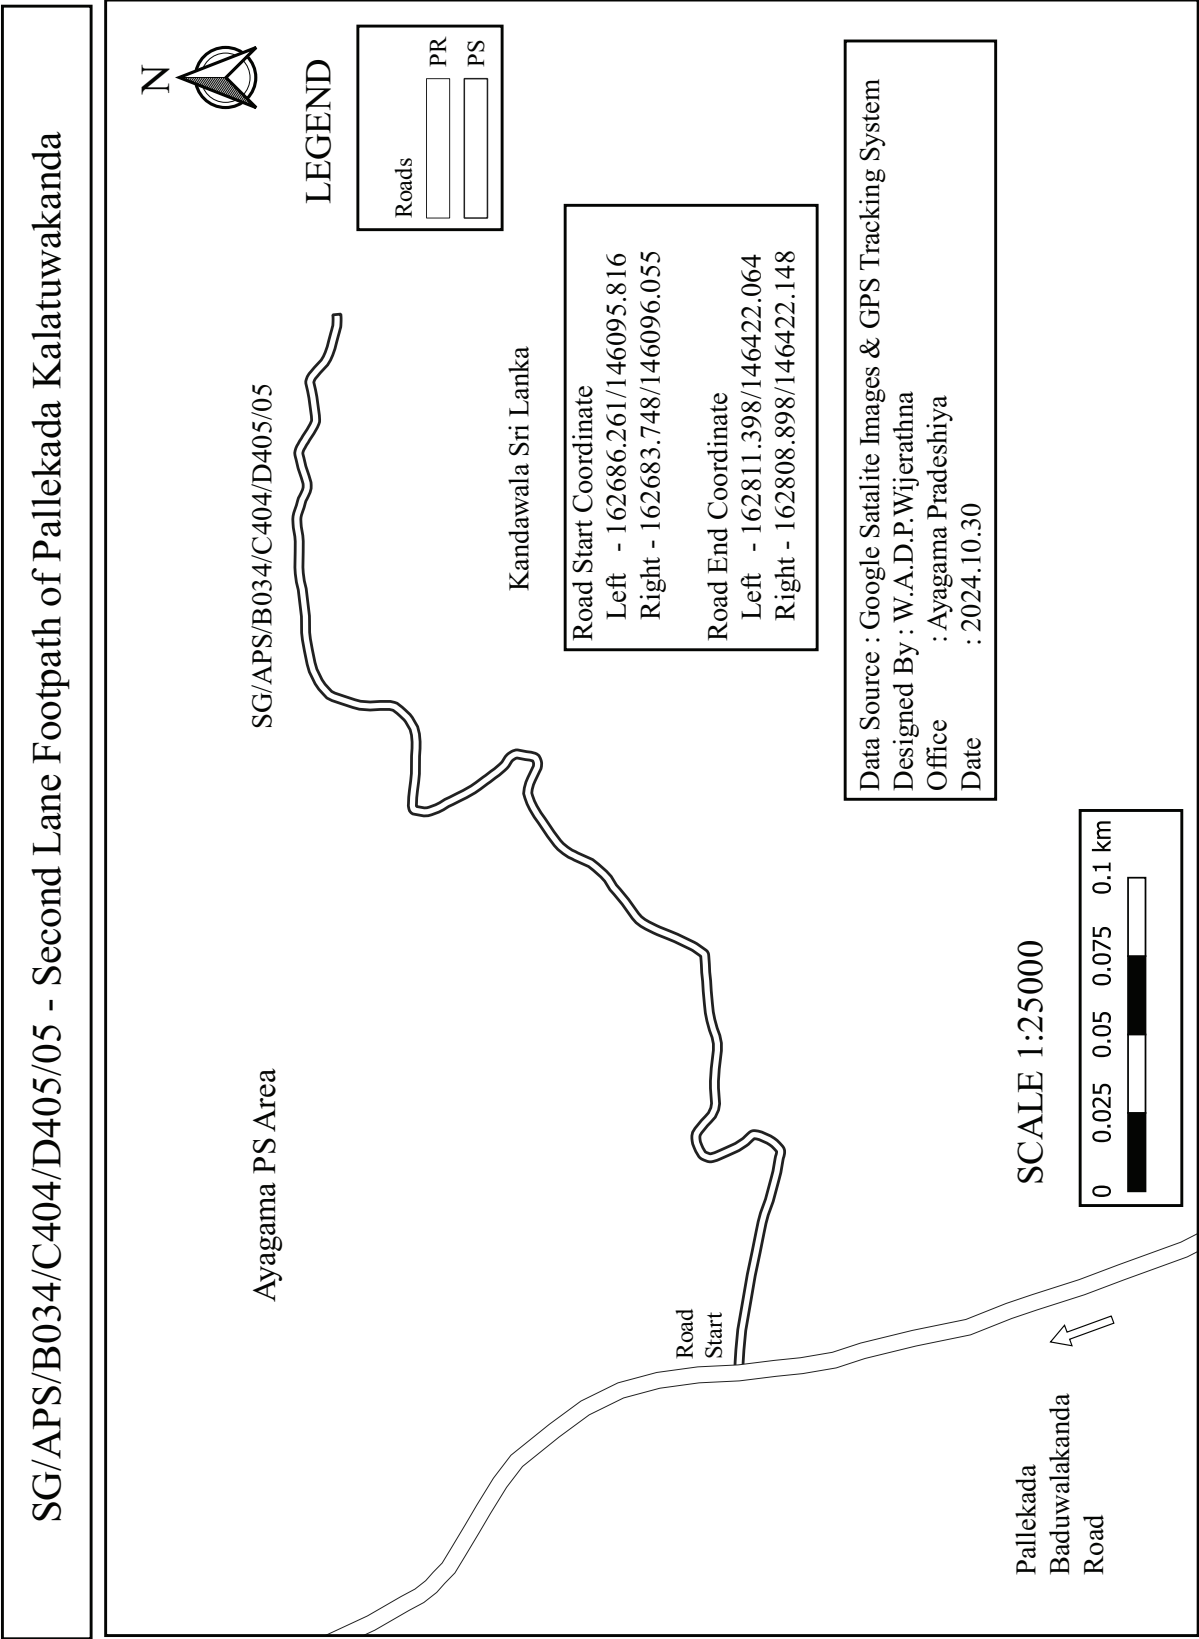

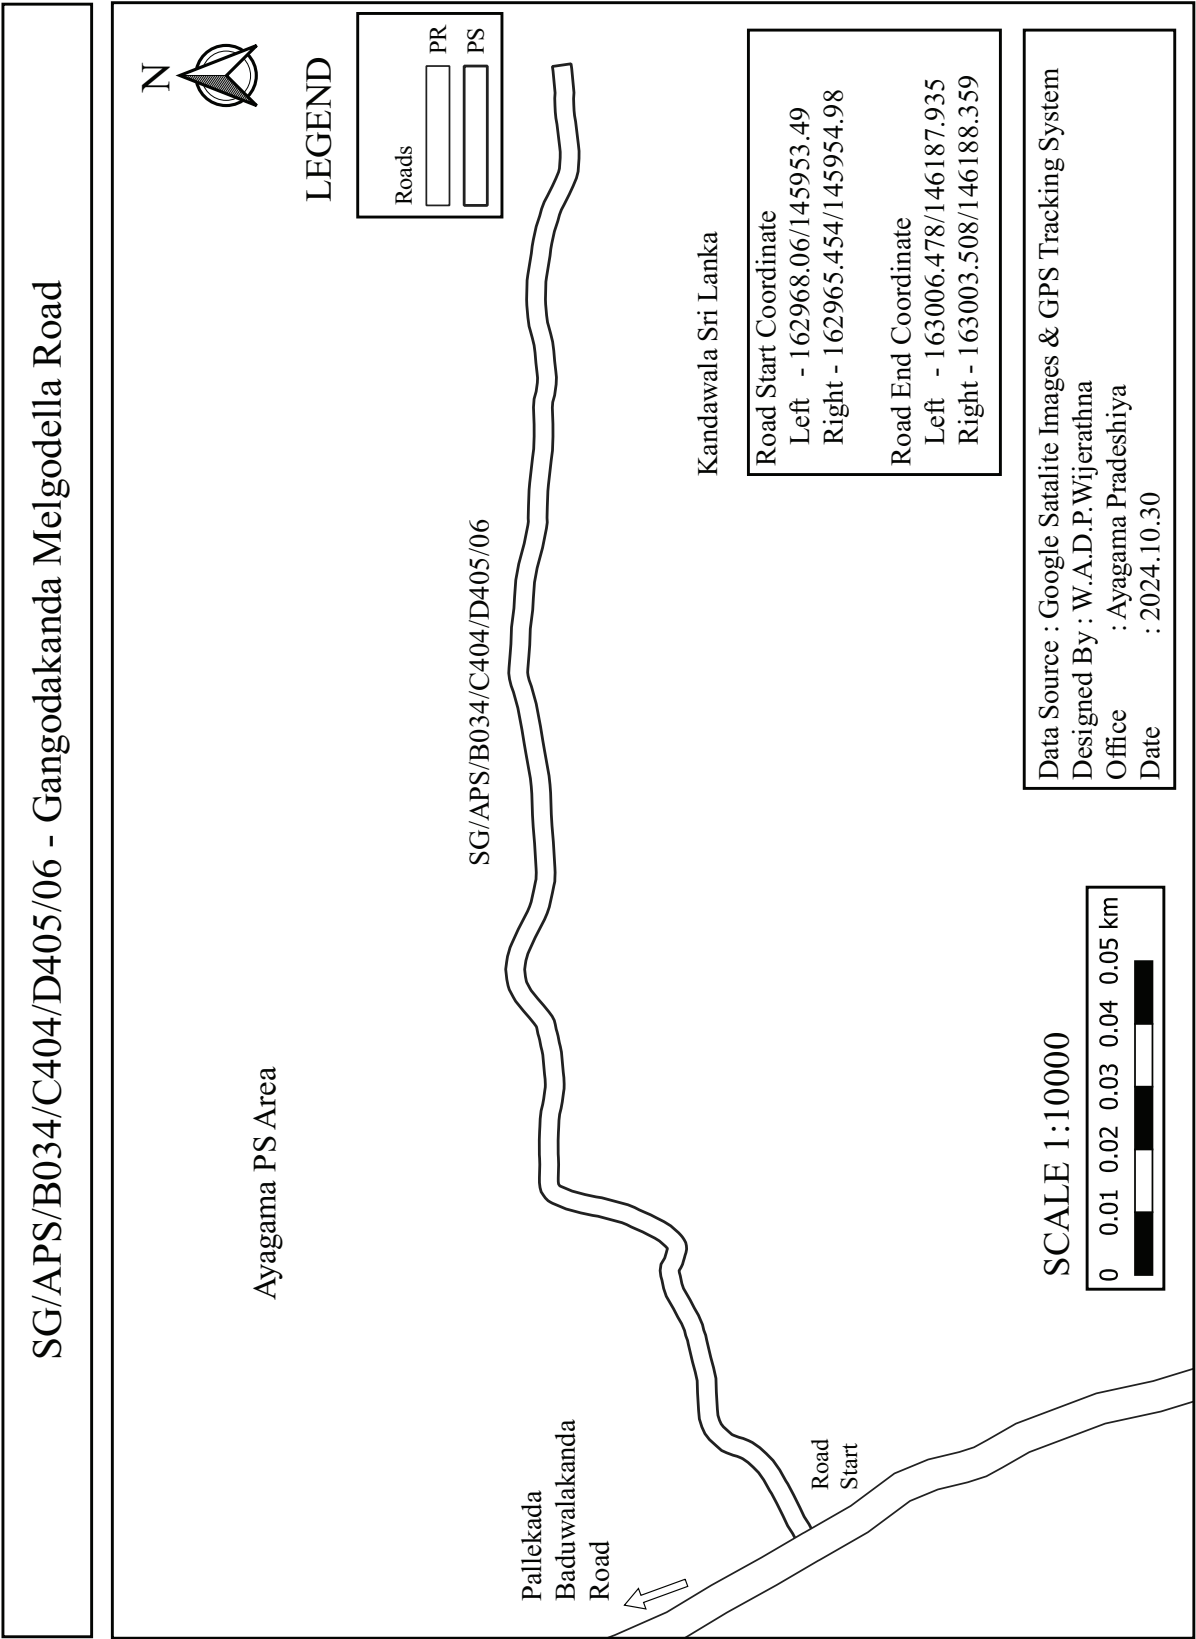


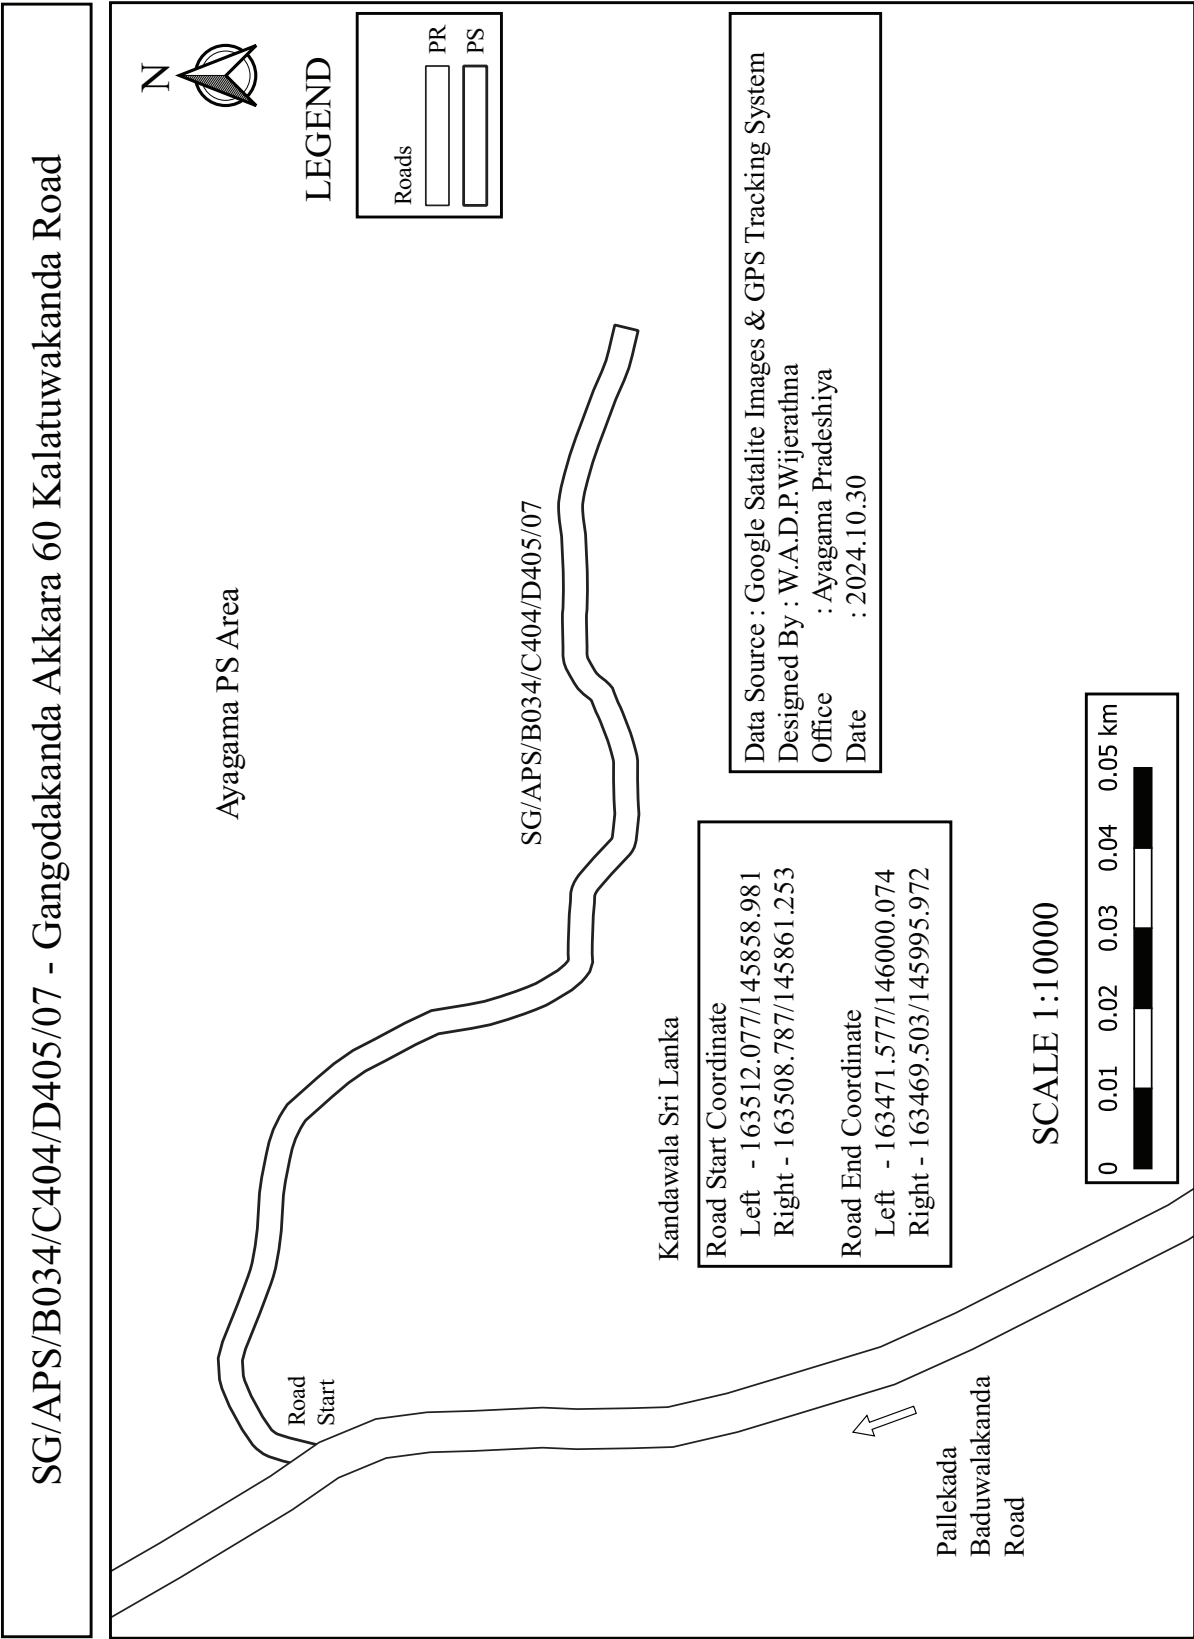


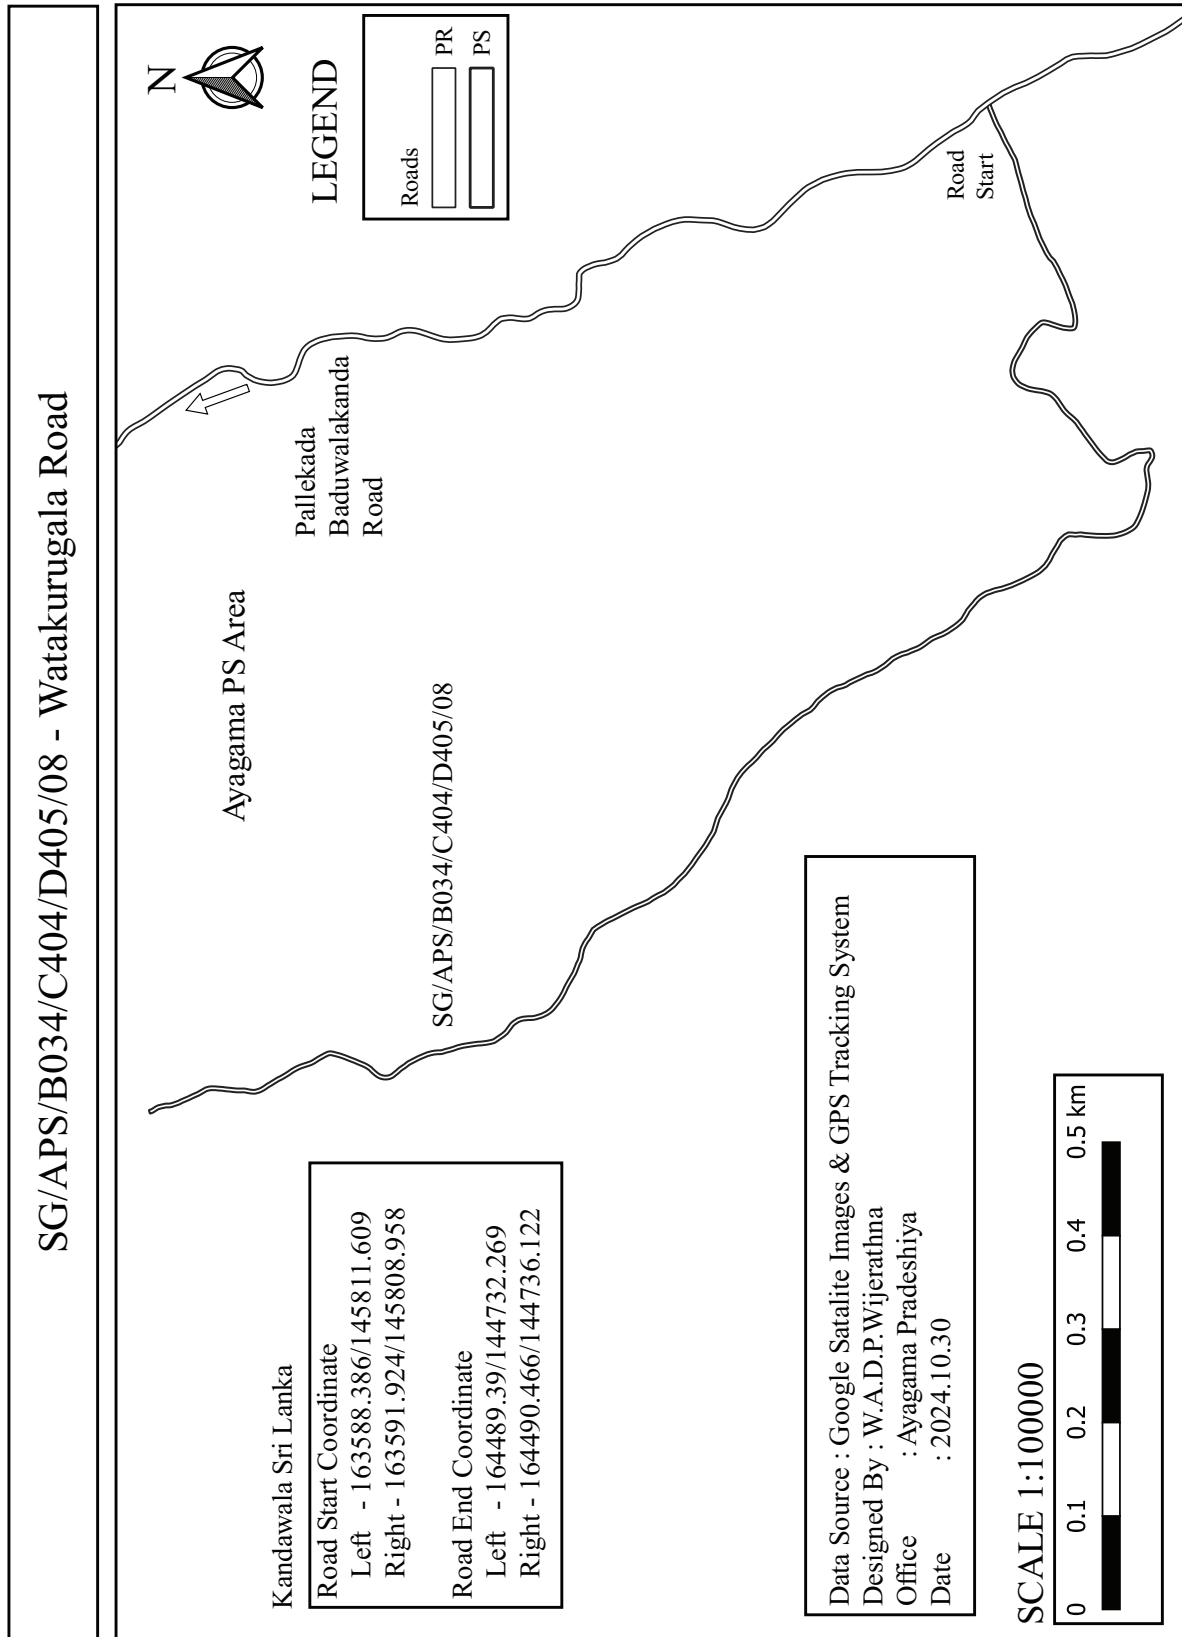

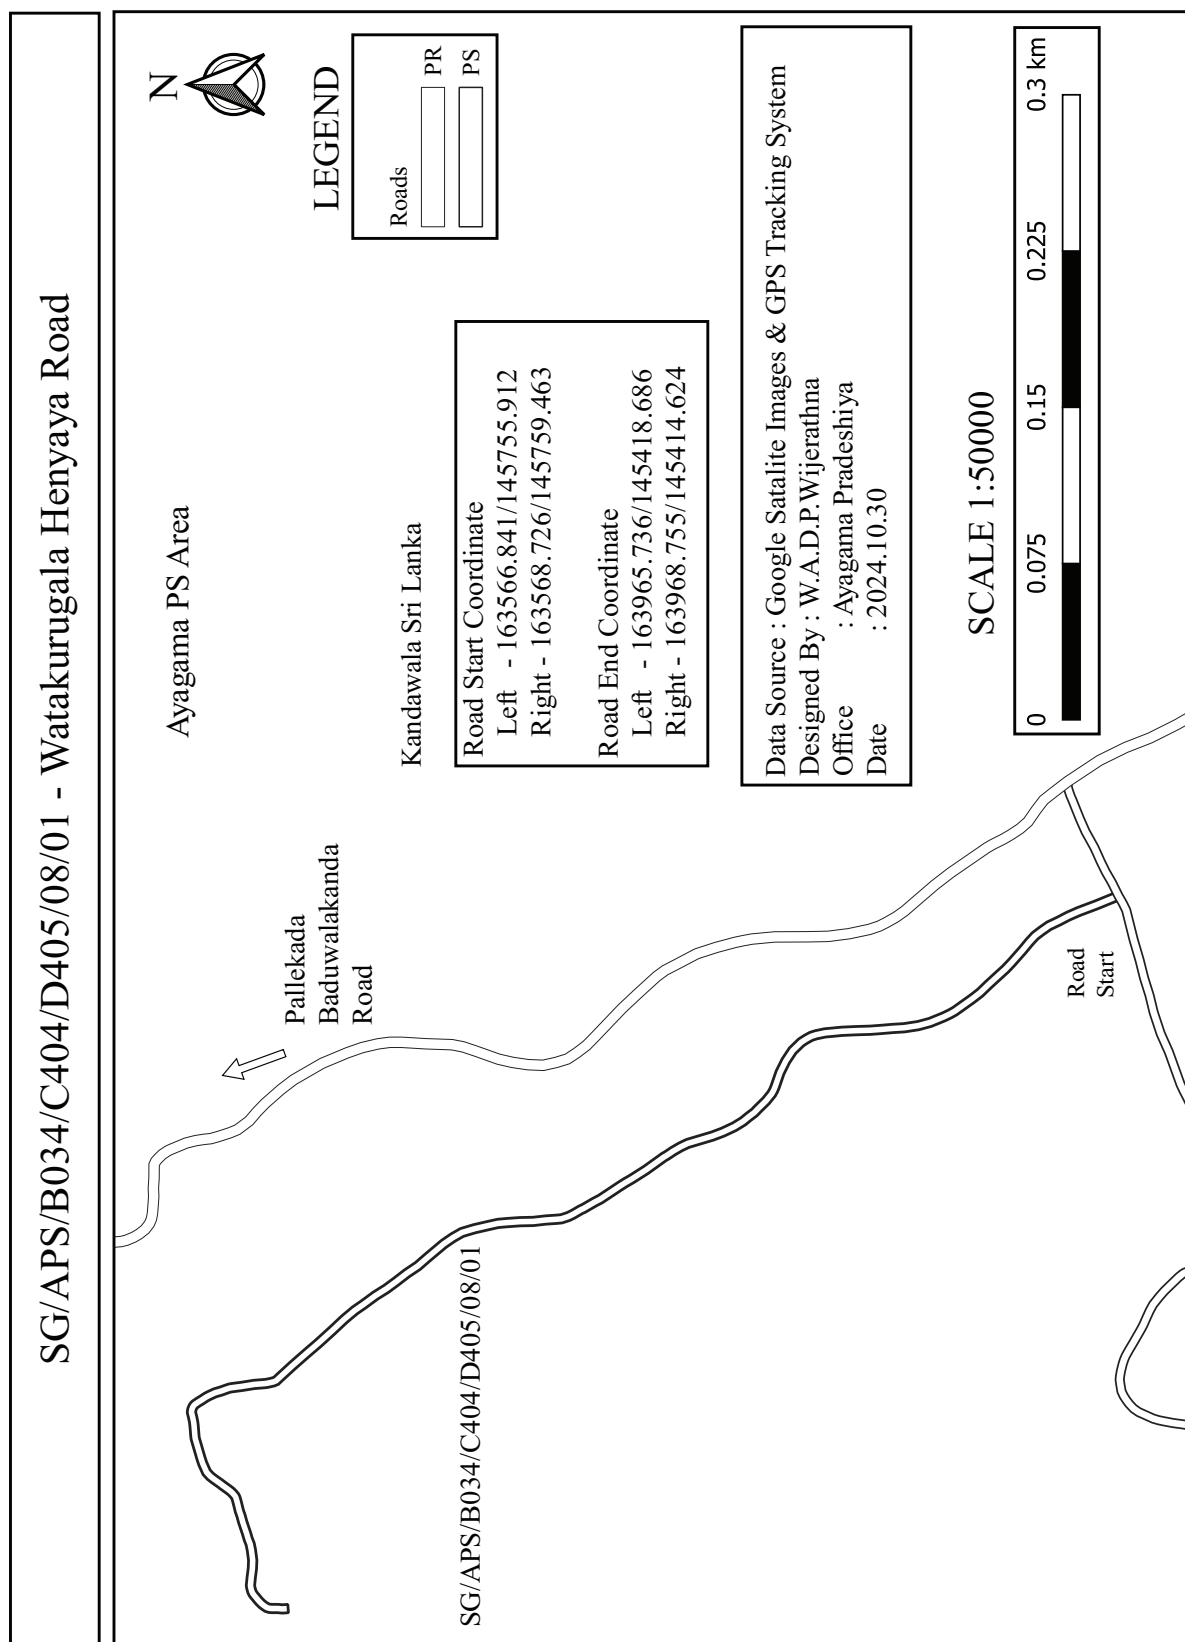





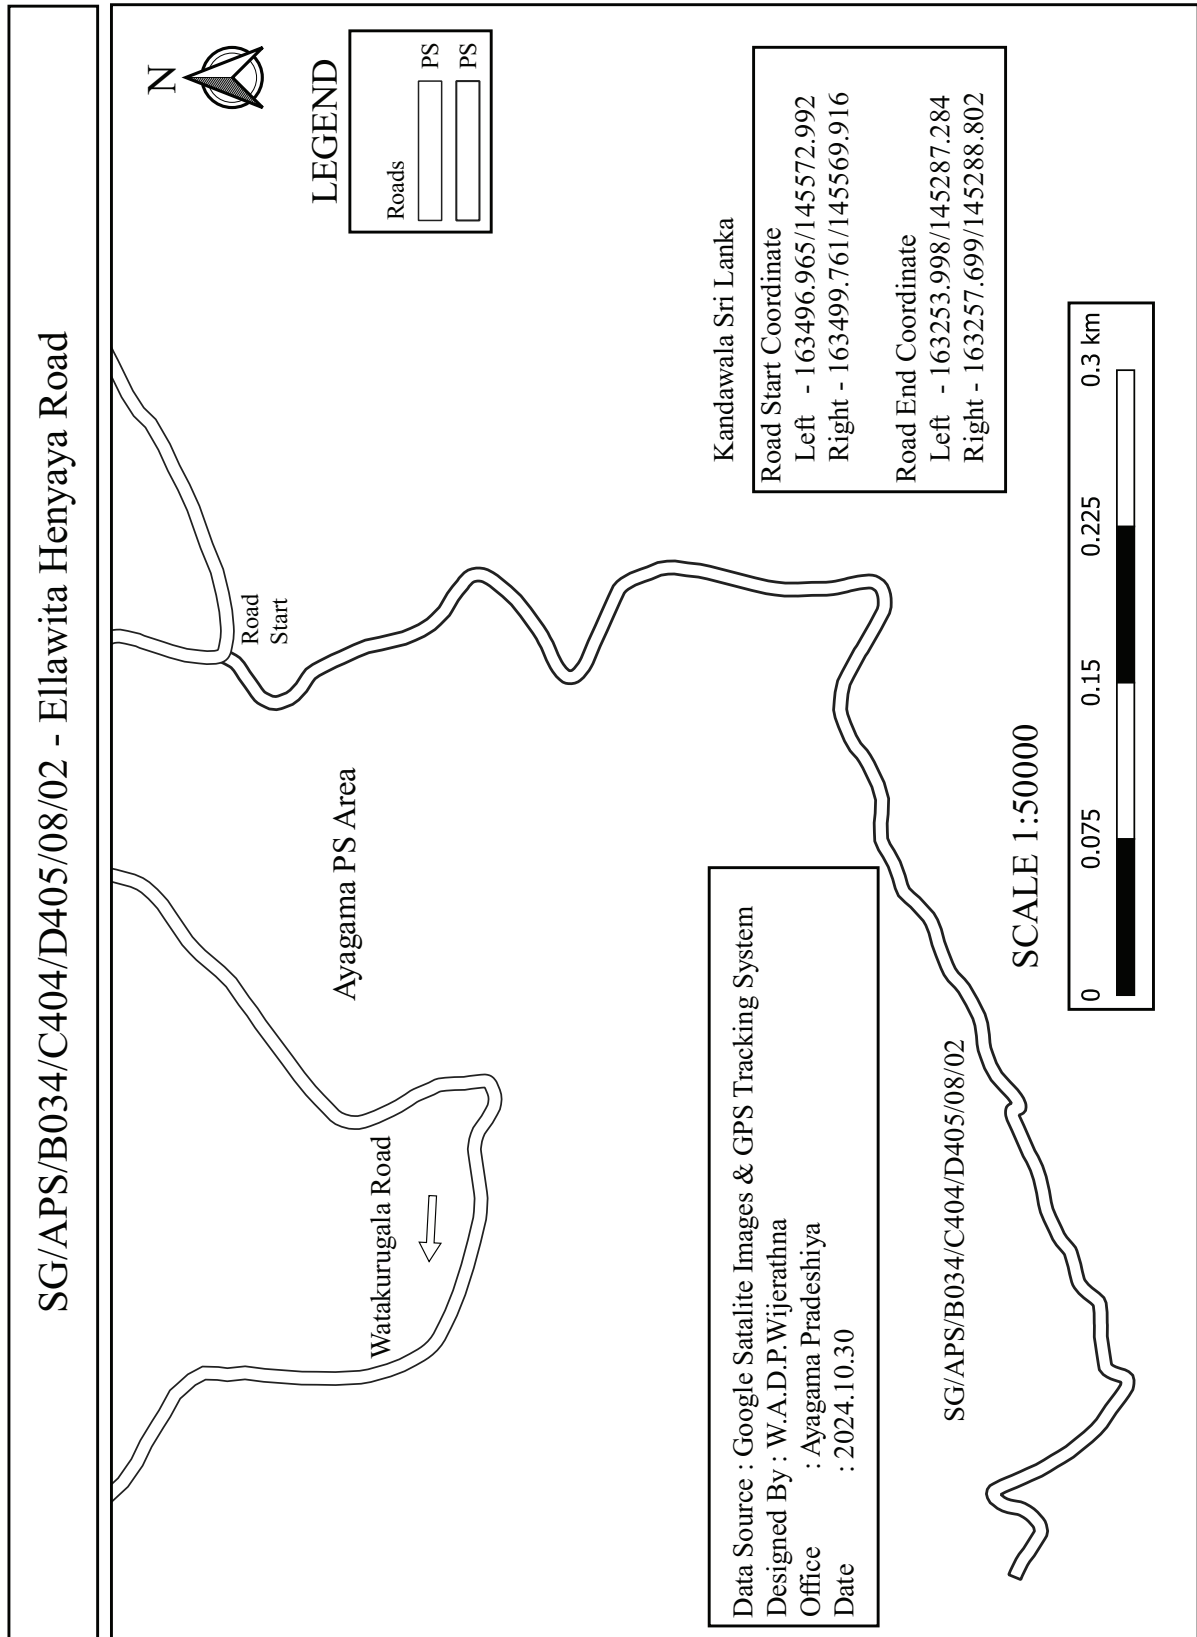


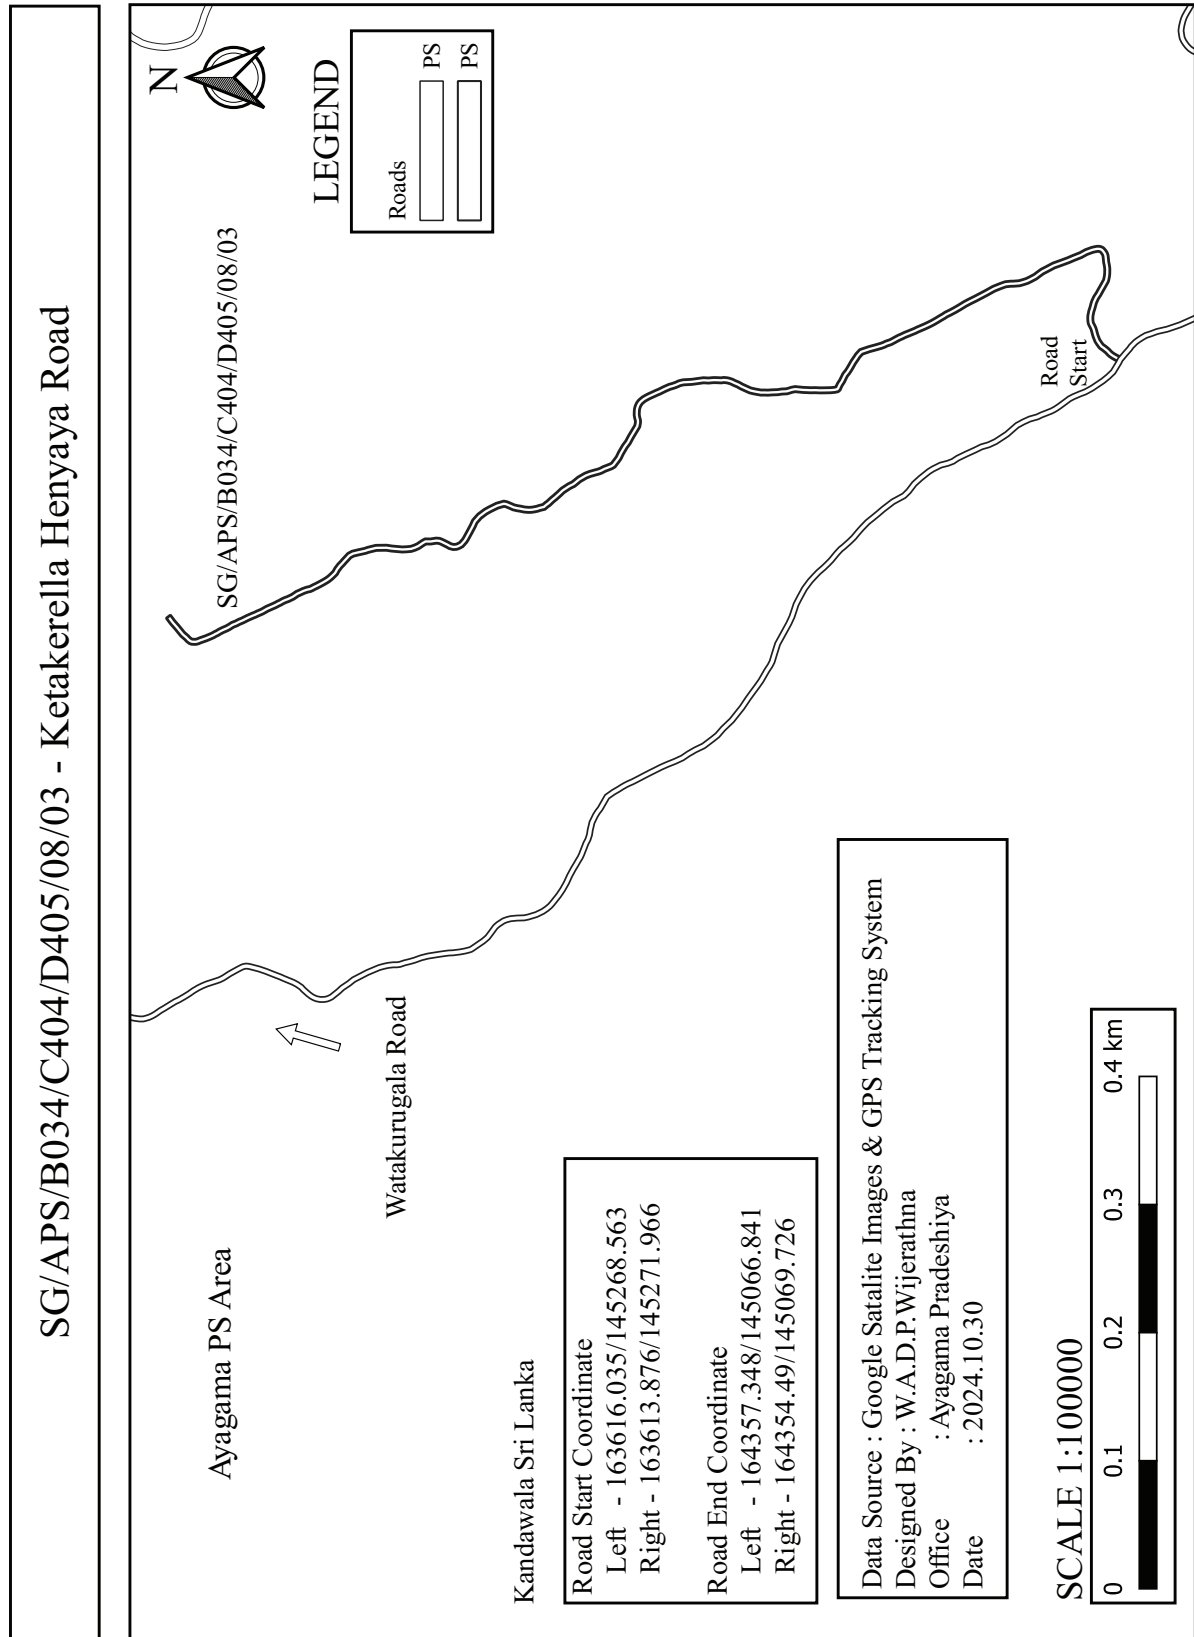



SG/APS/B034/C404/D405/08/03/01 - Henyaya Ketakerella Pahala Road

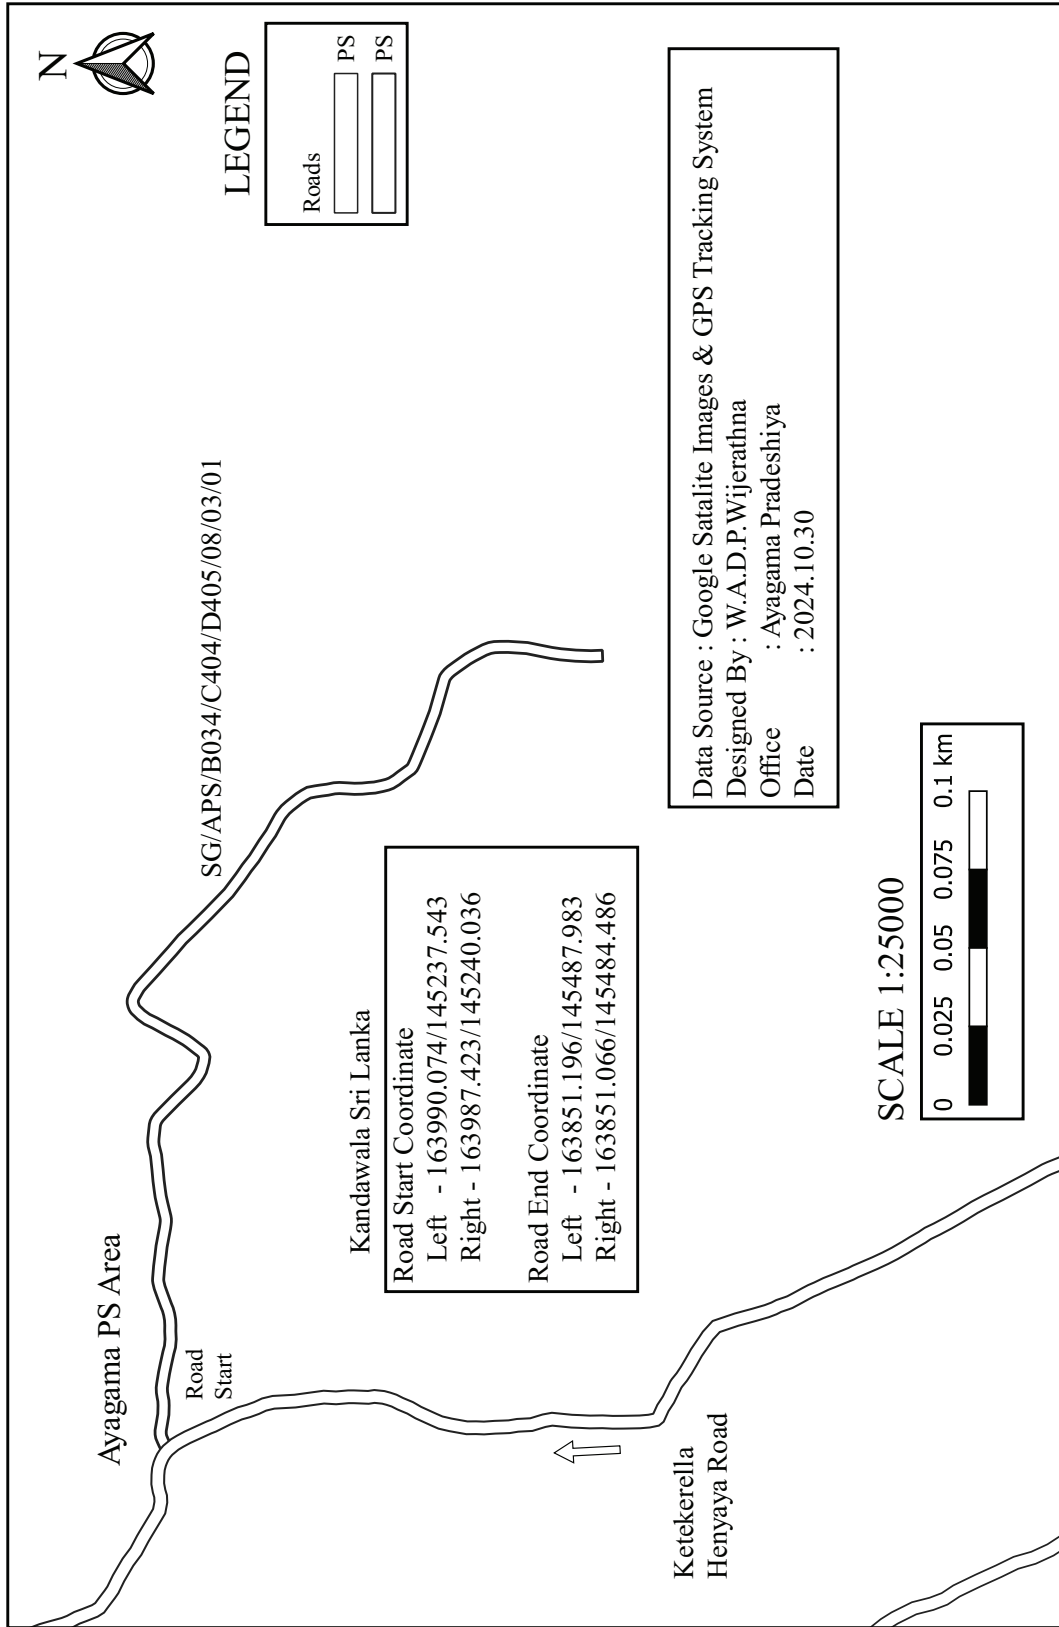


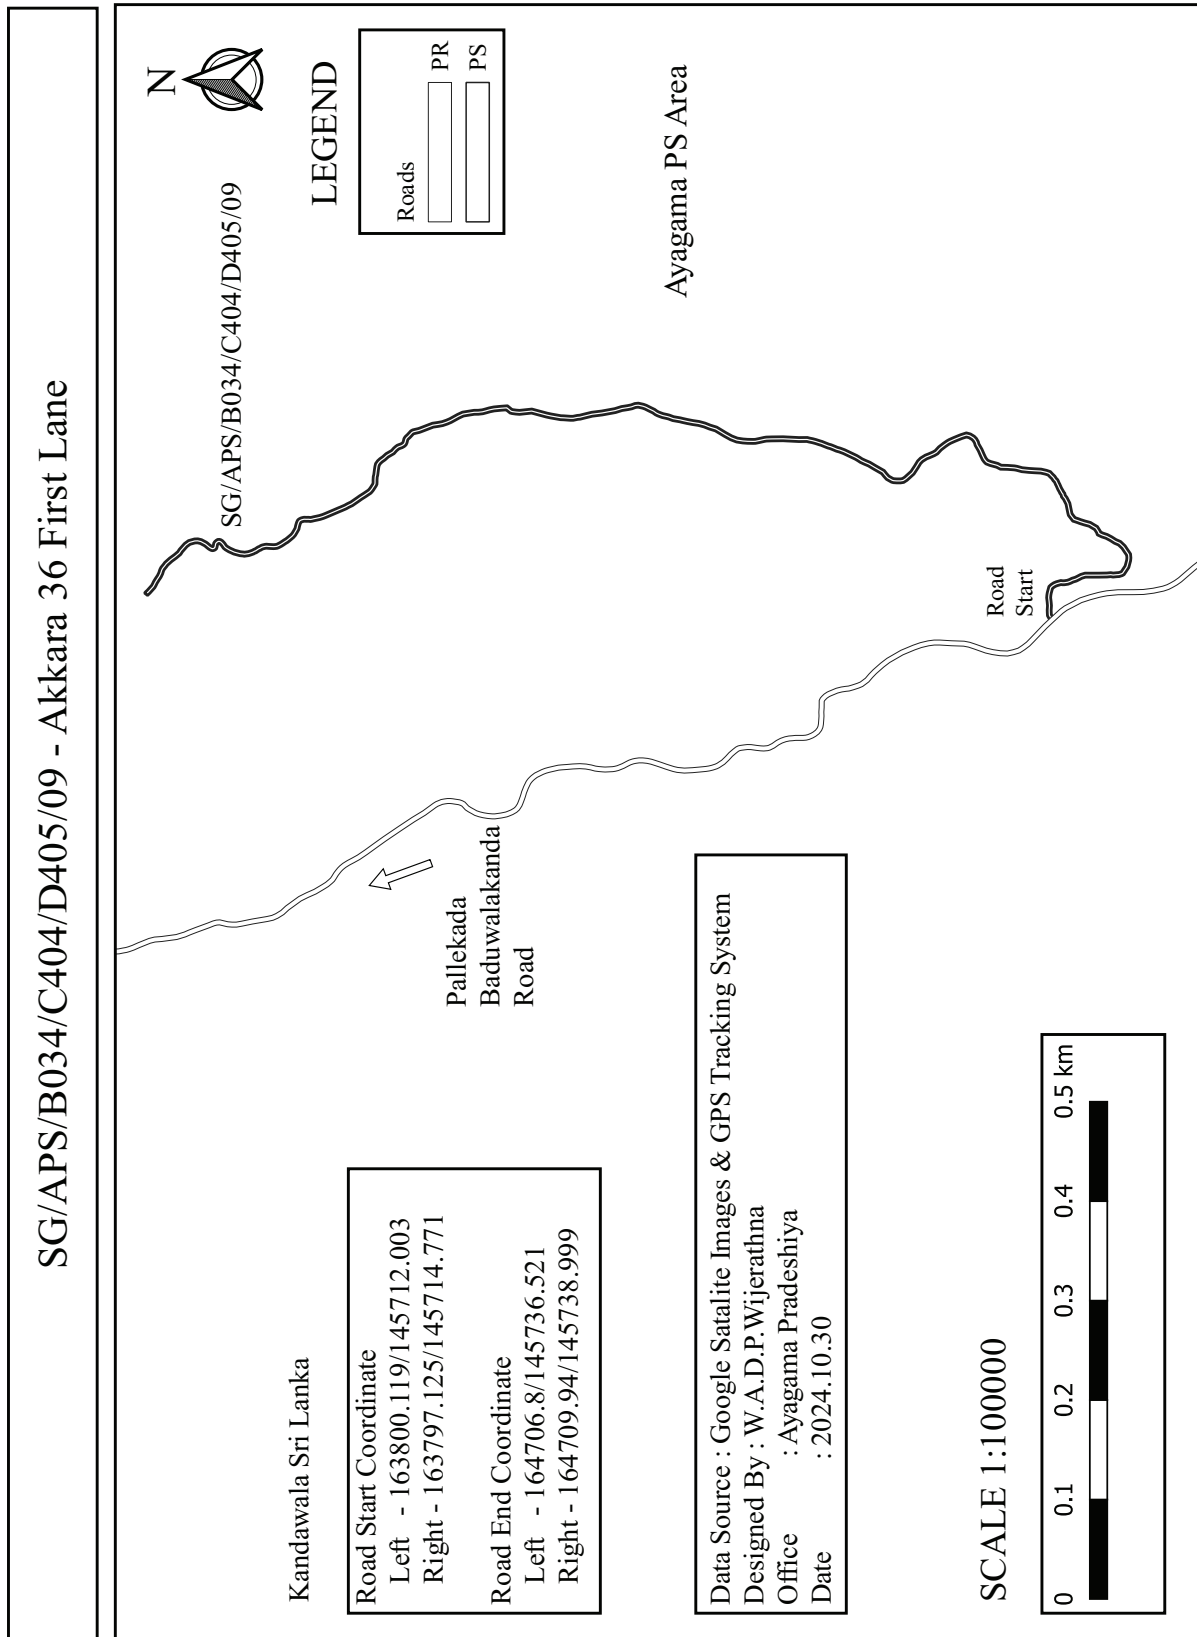

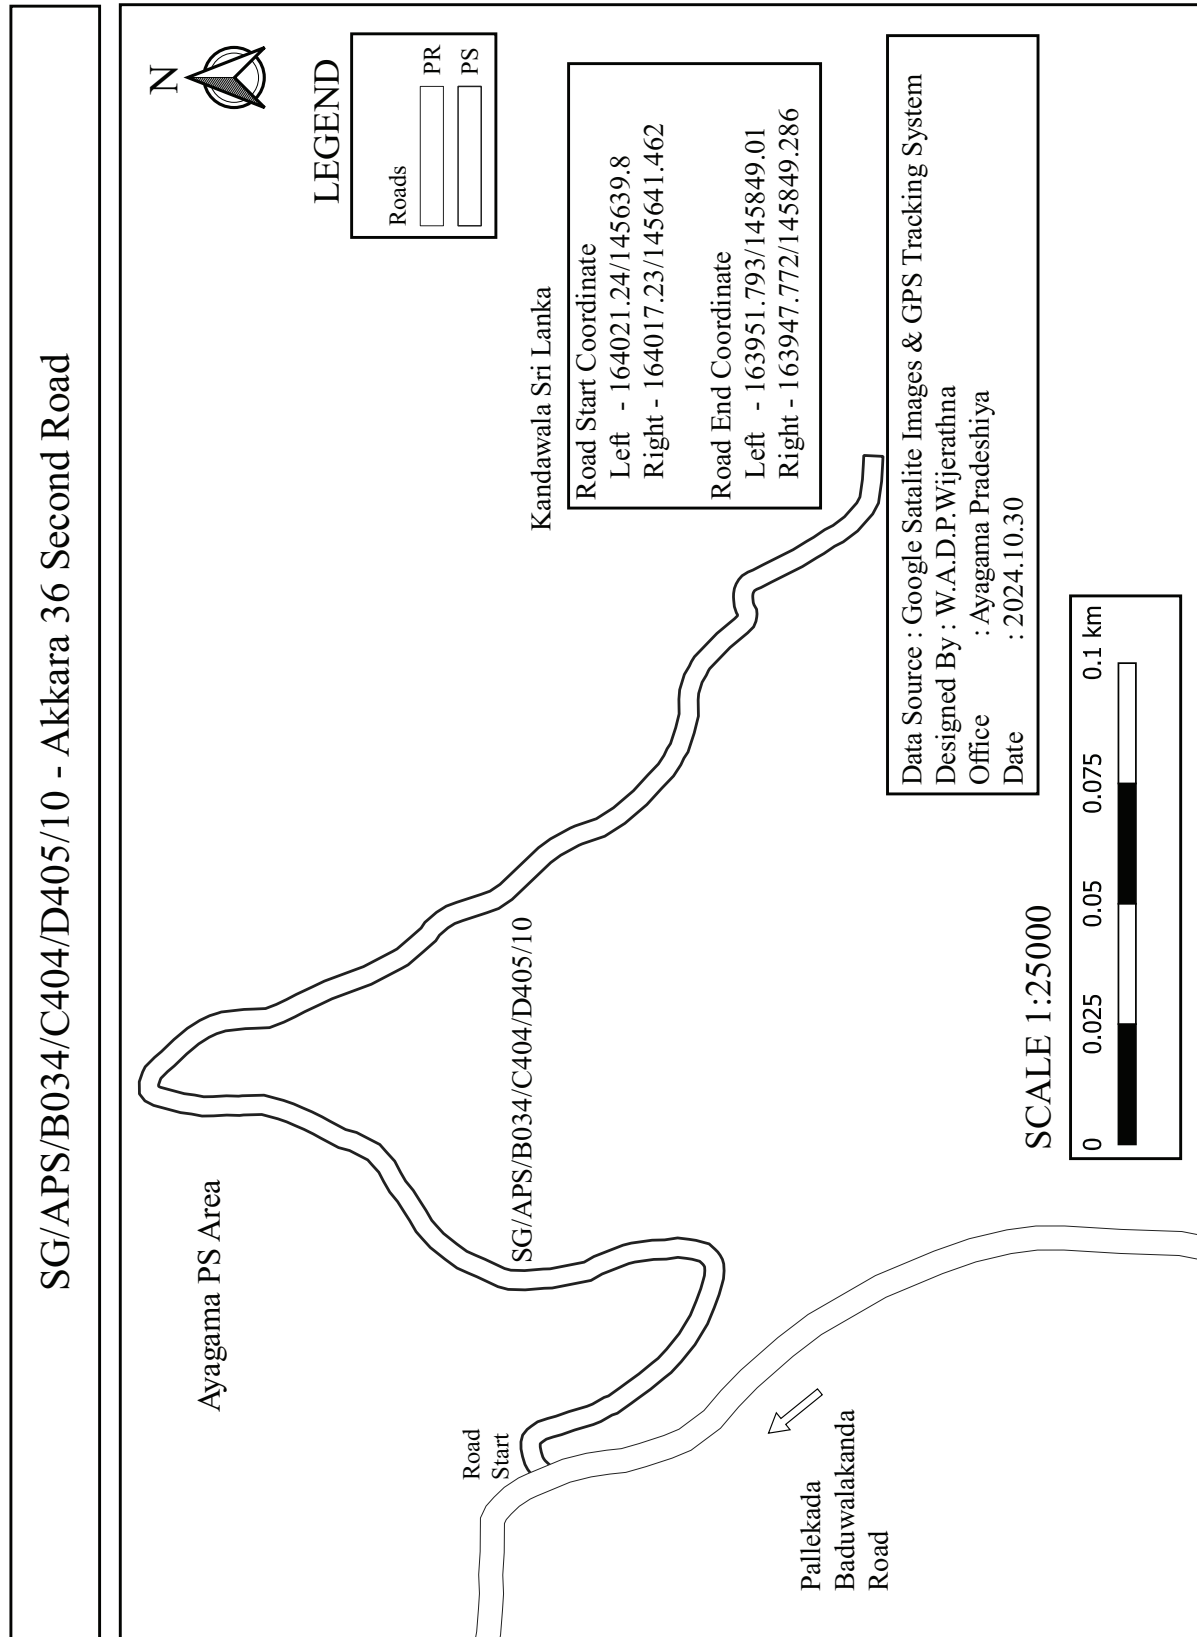


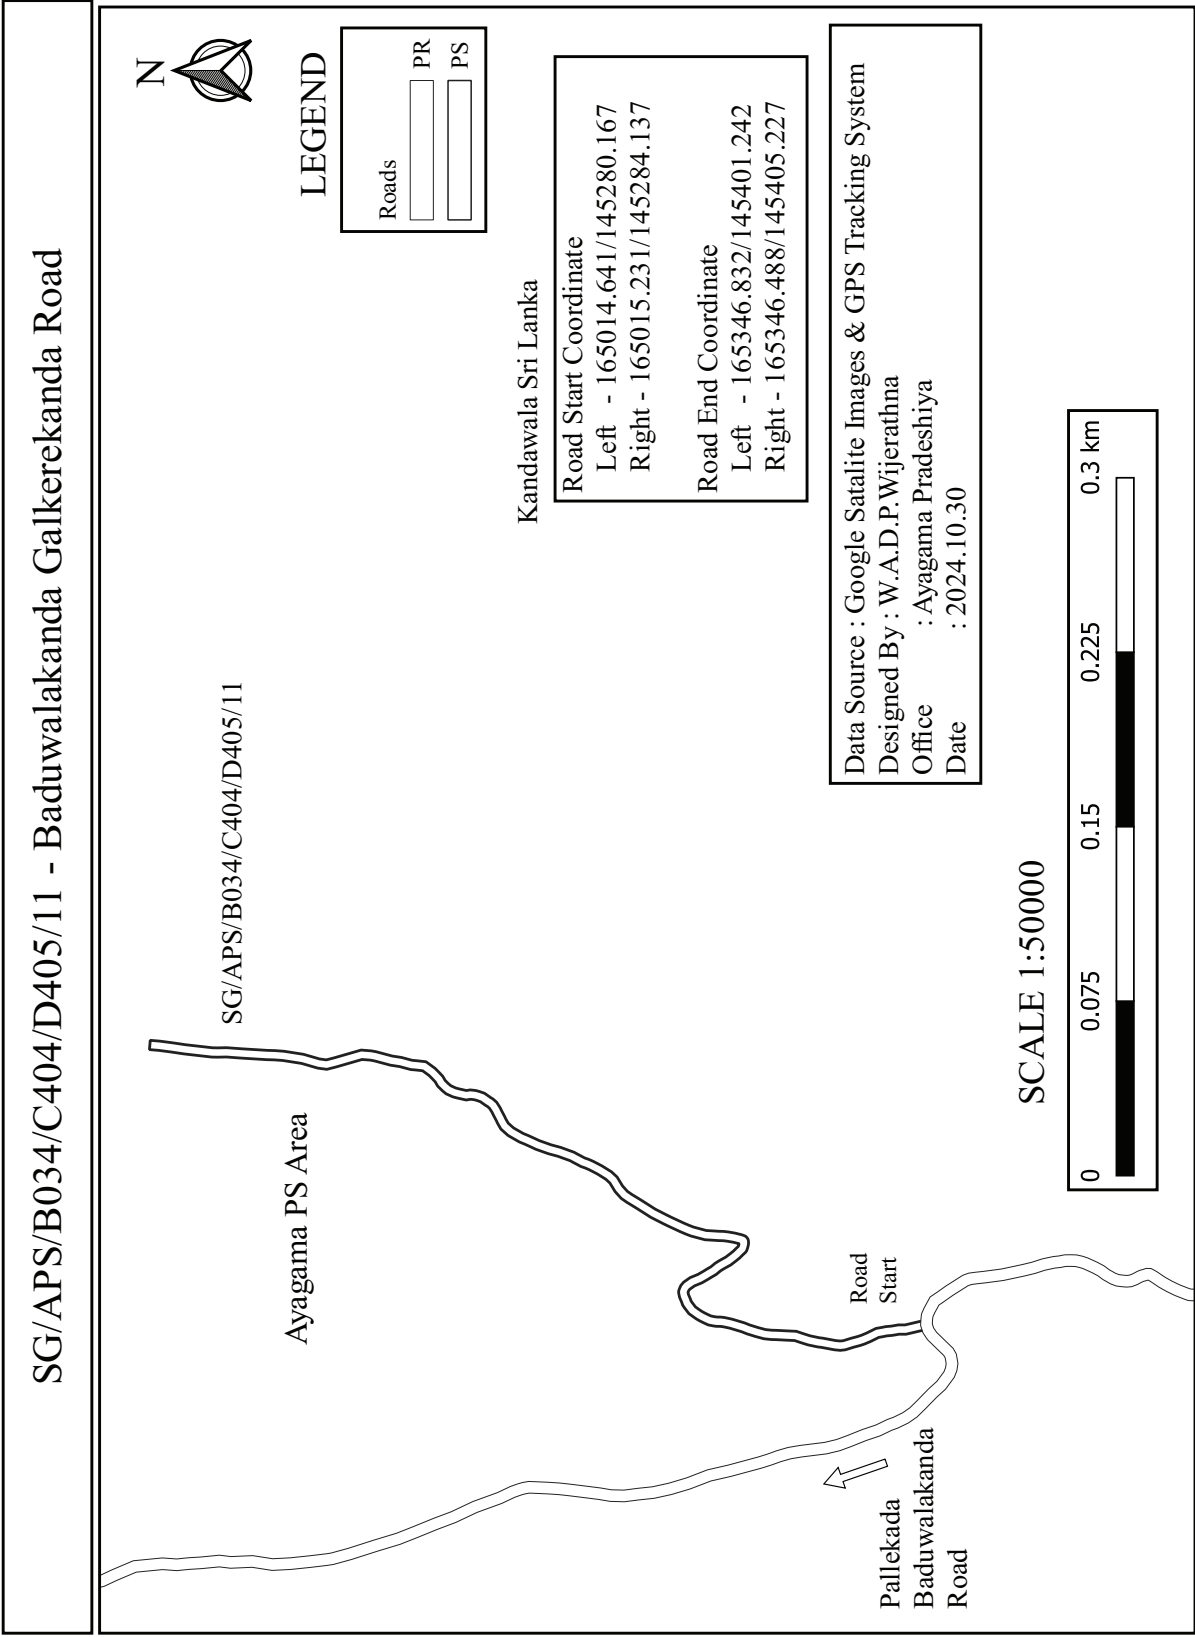


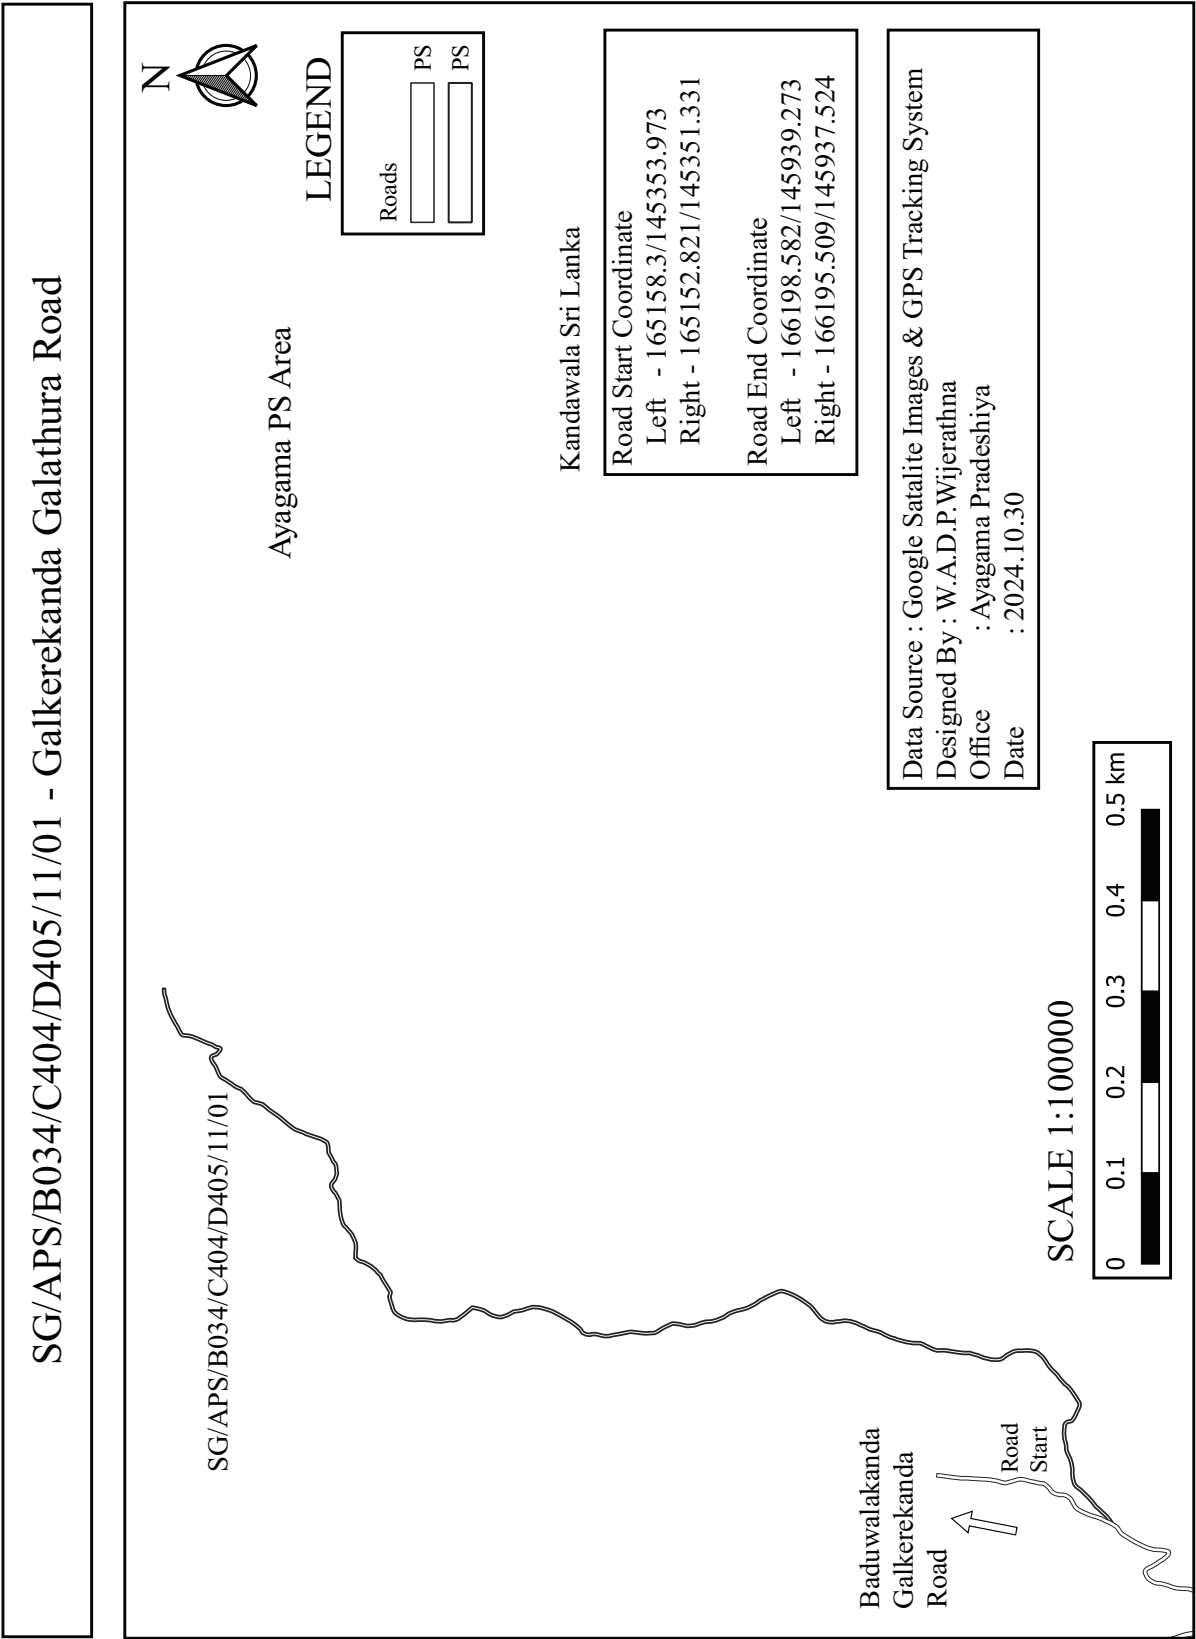


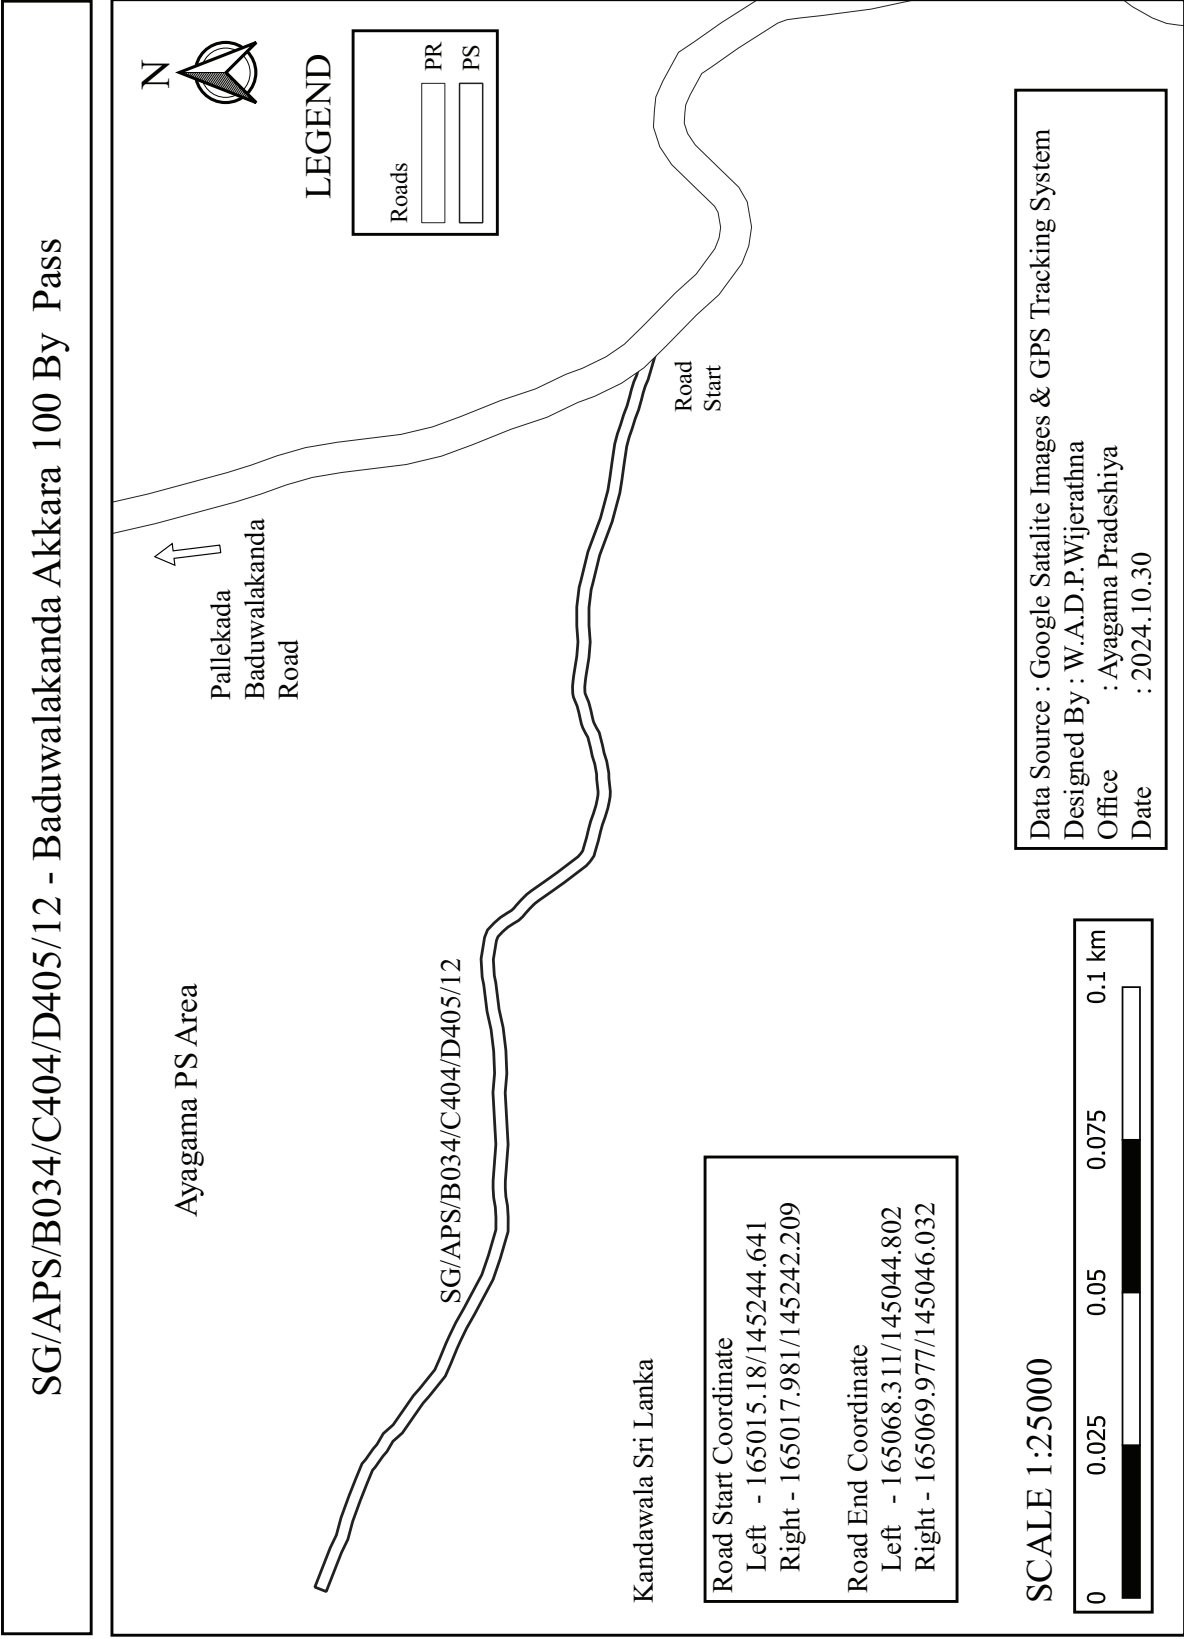





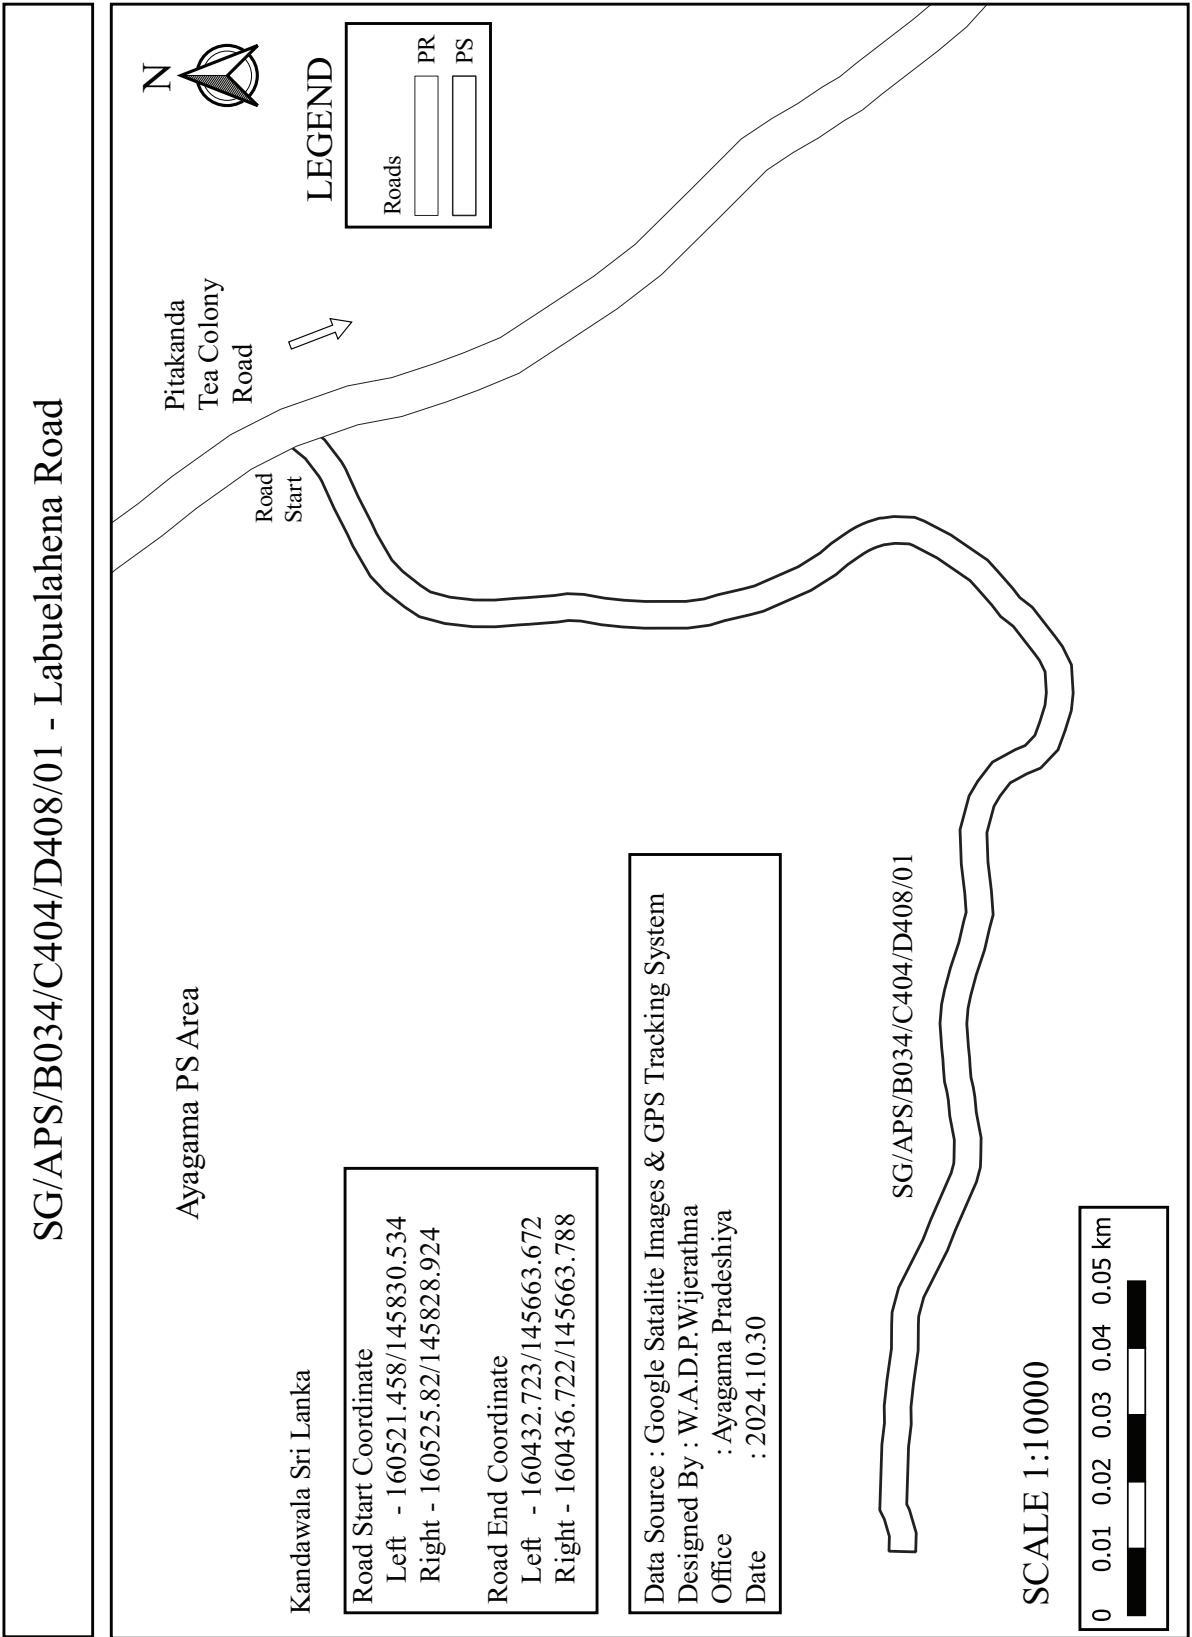


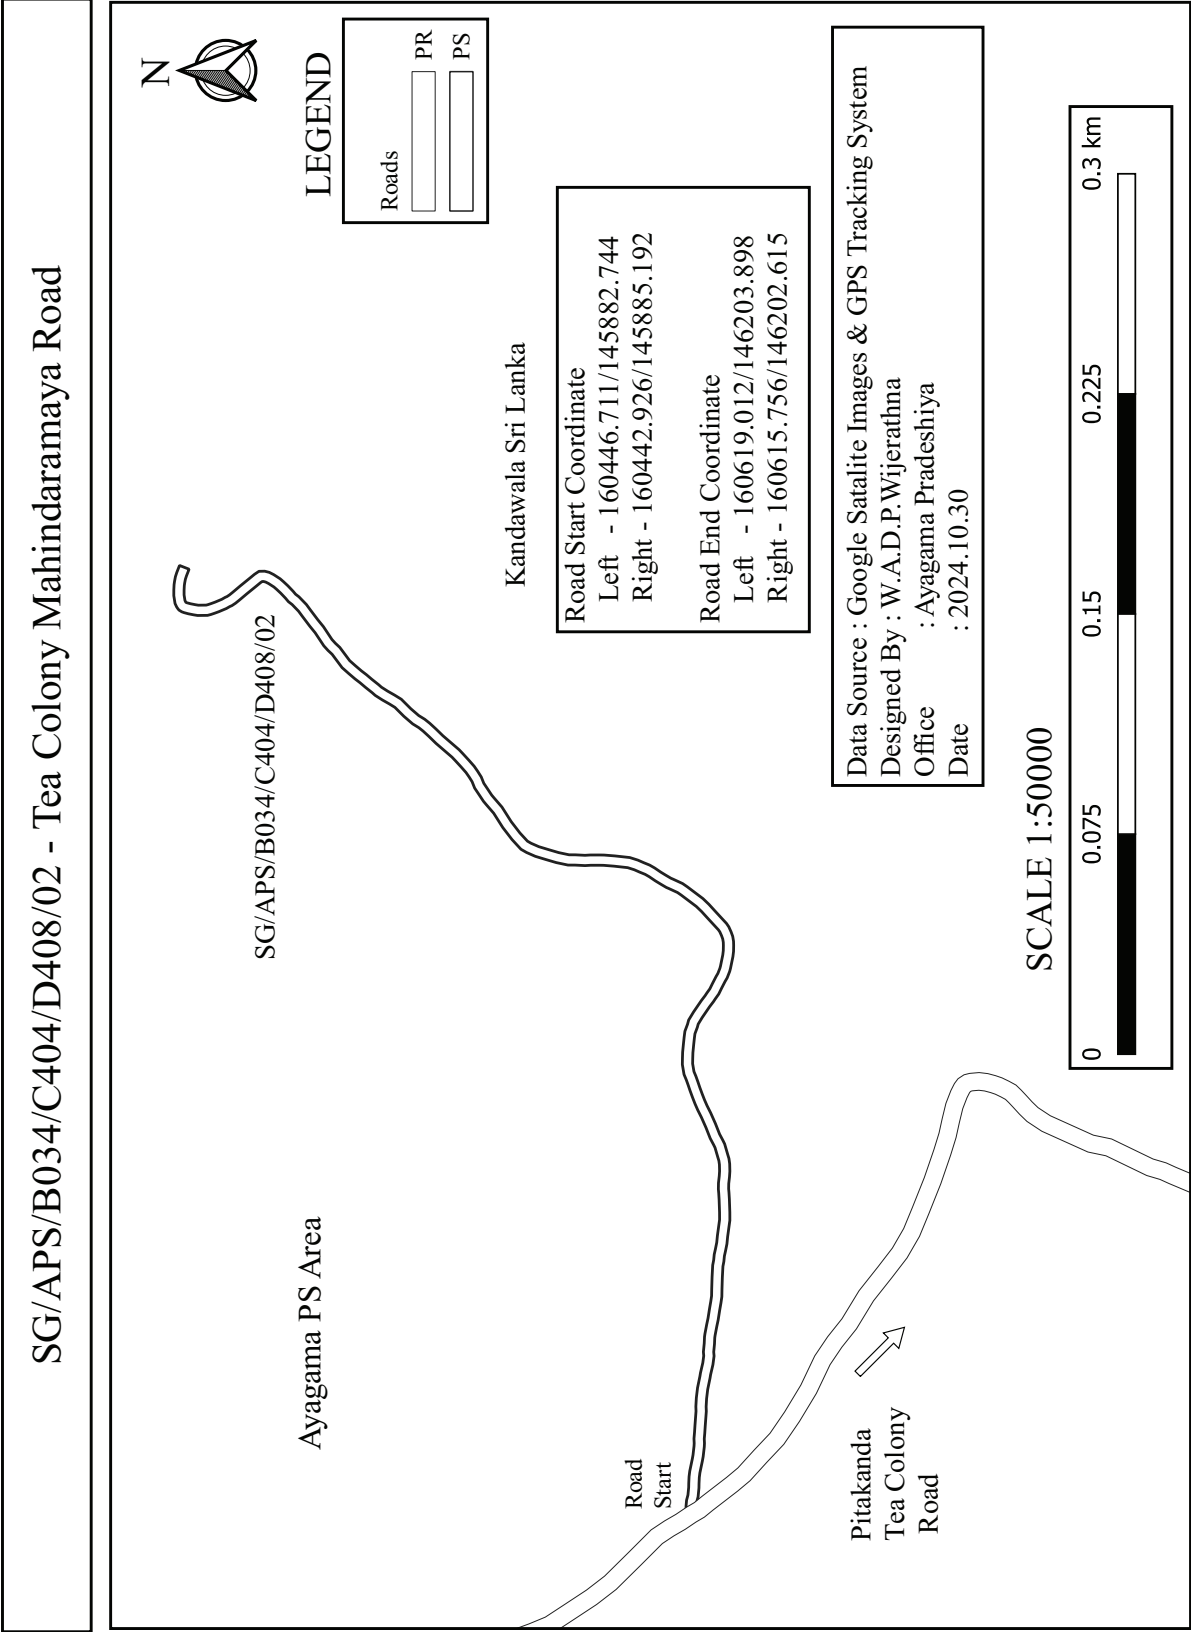


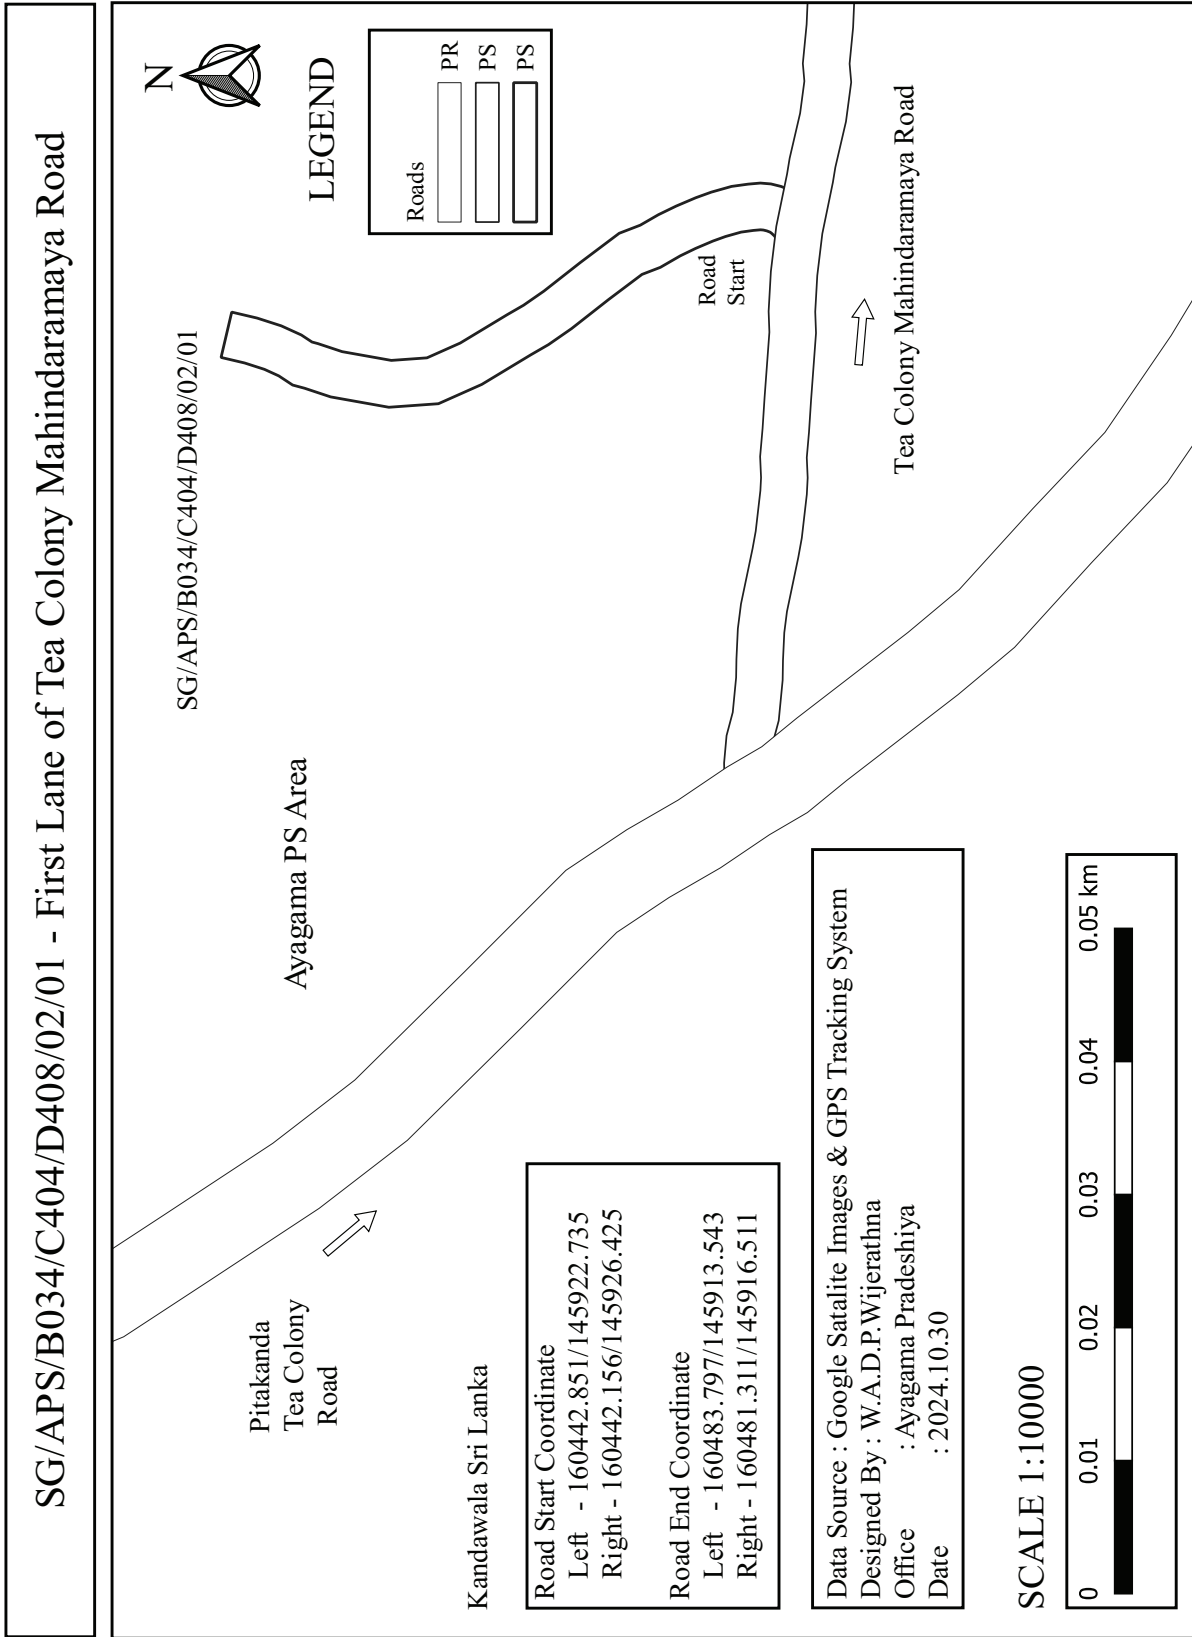


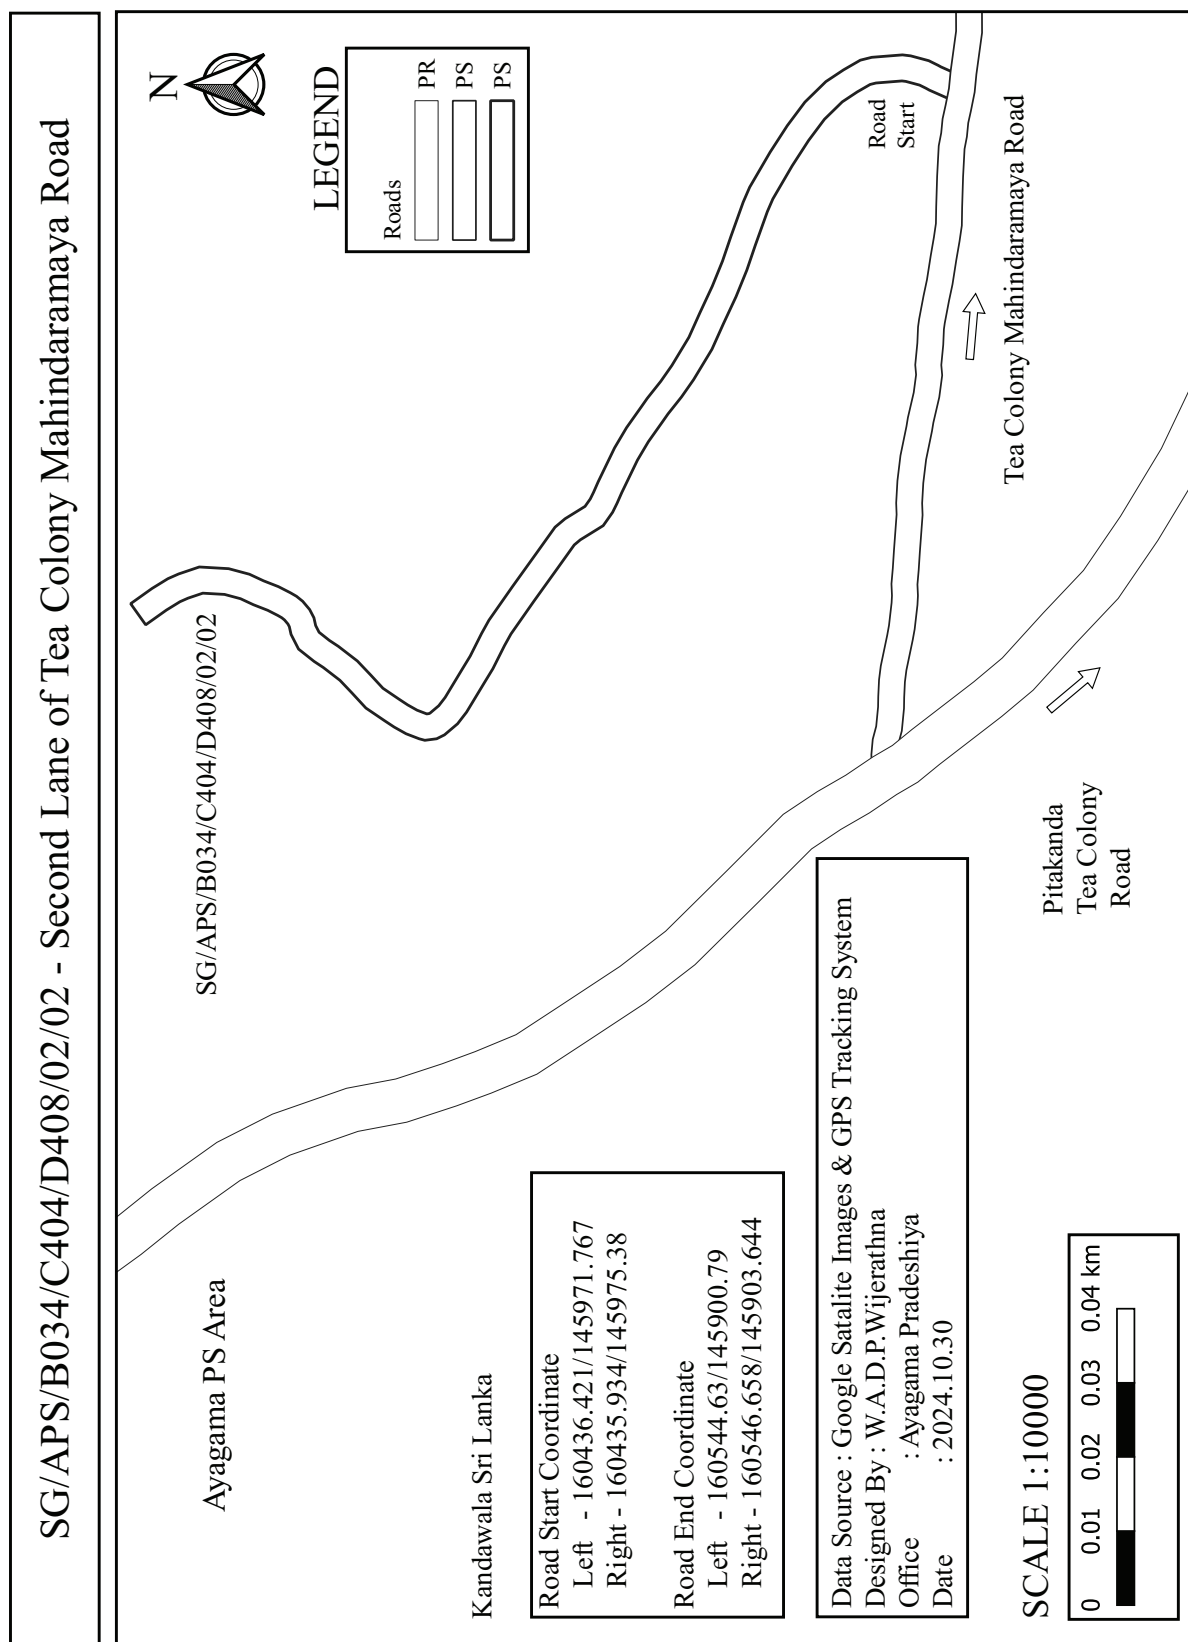

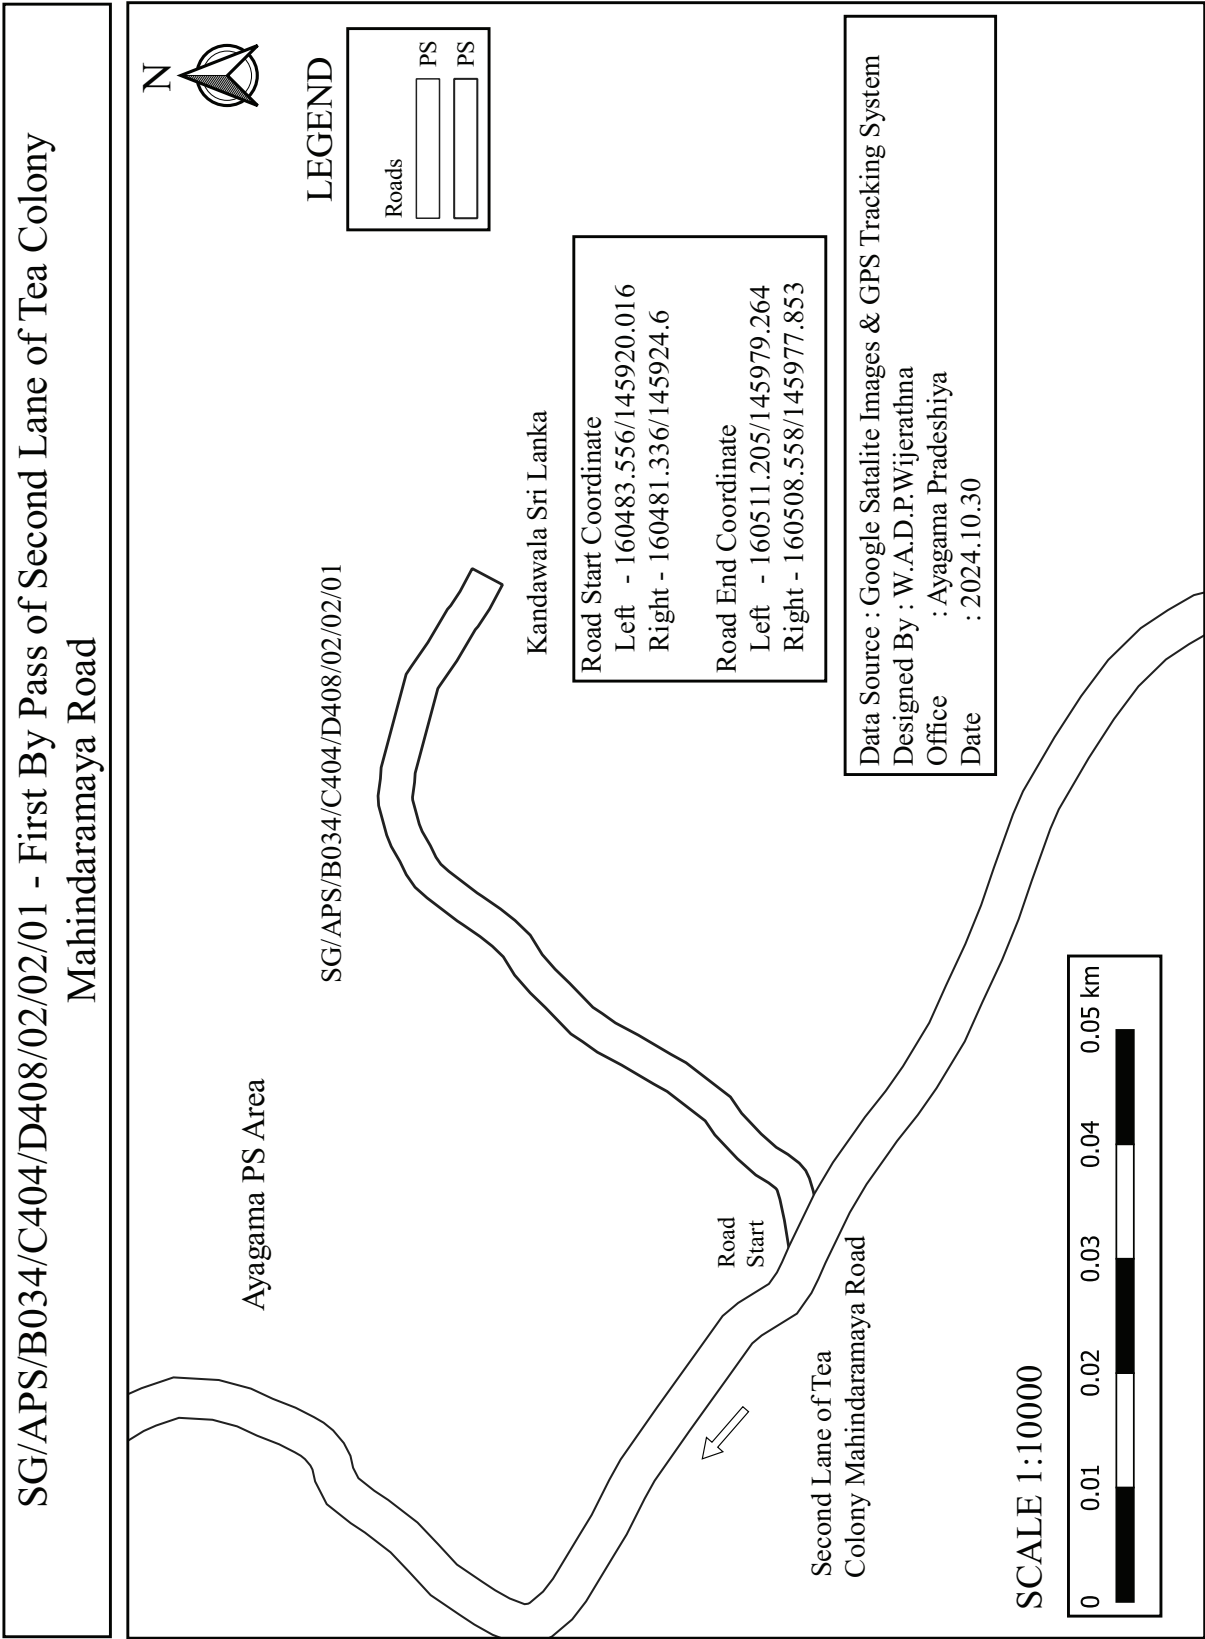


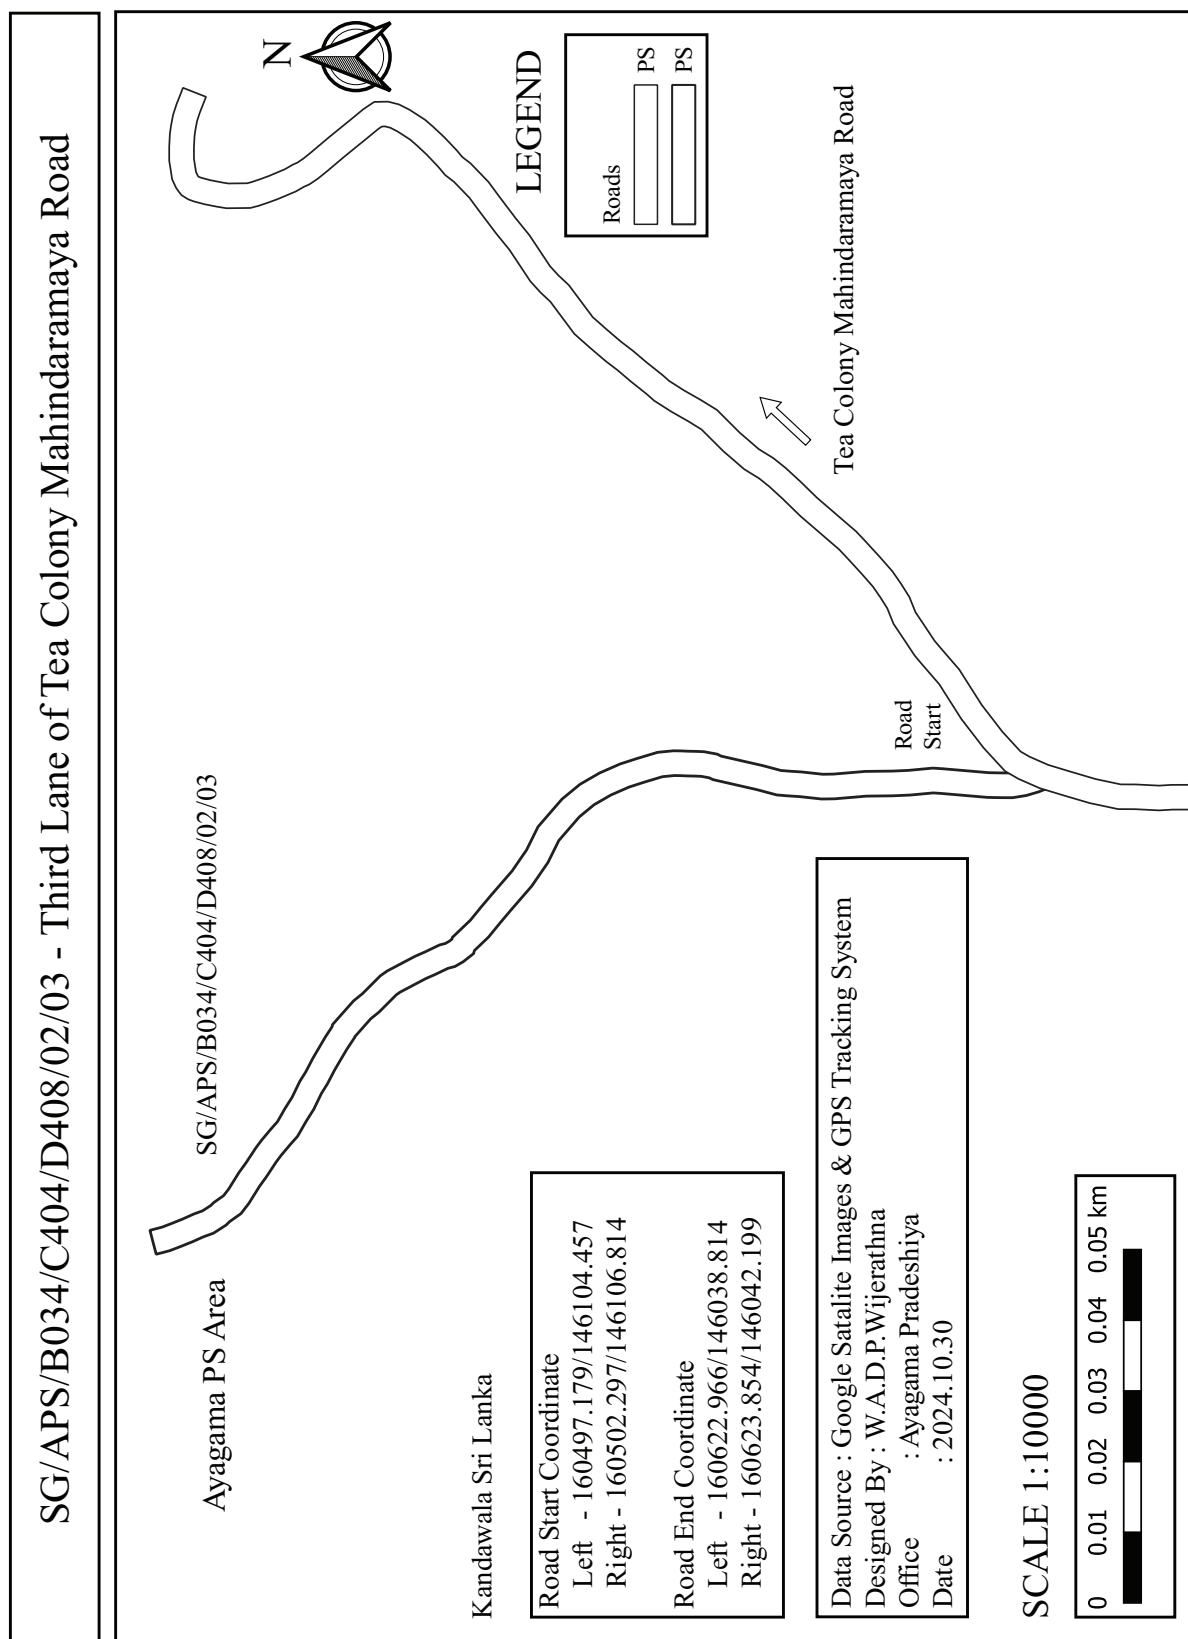


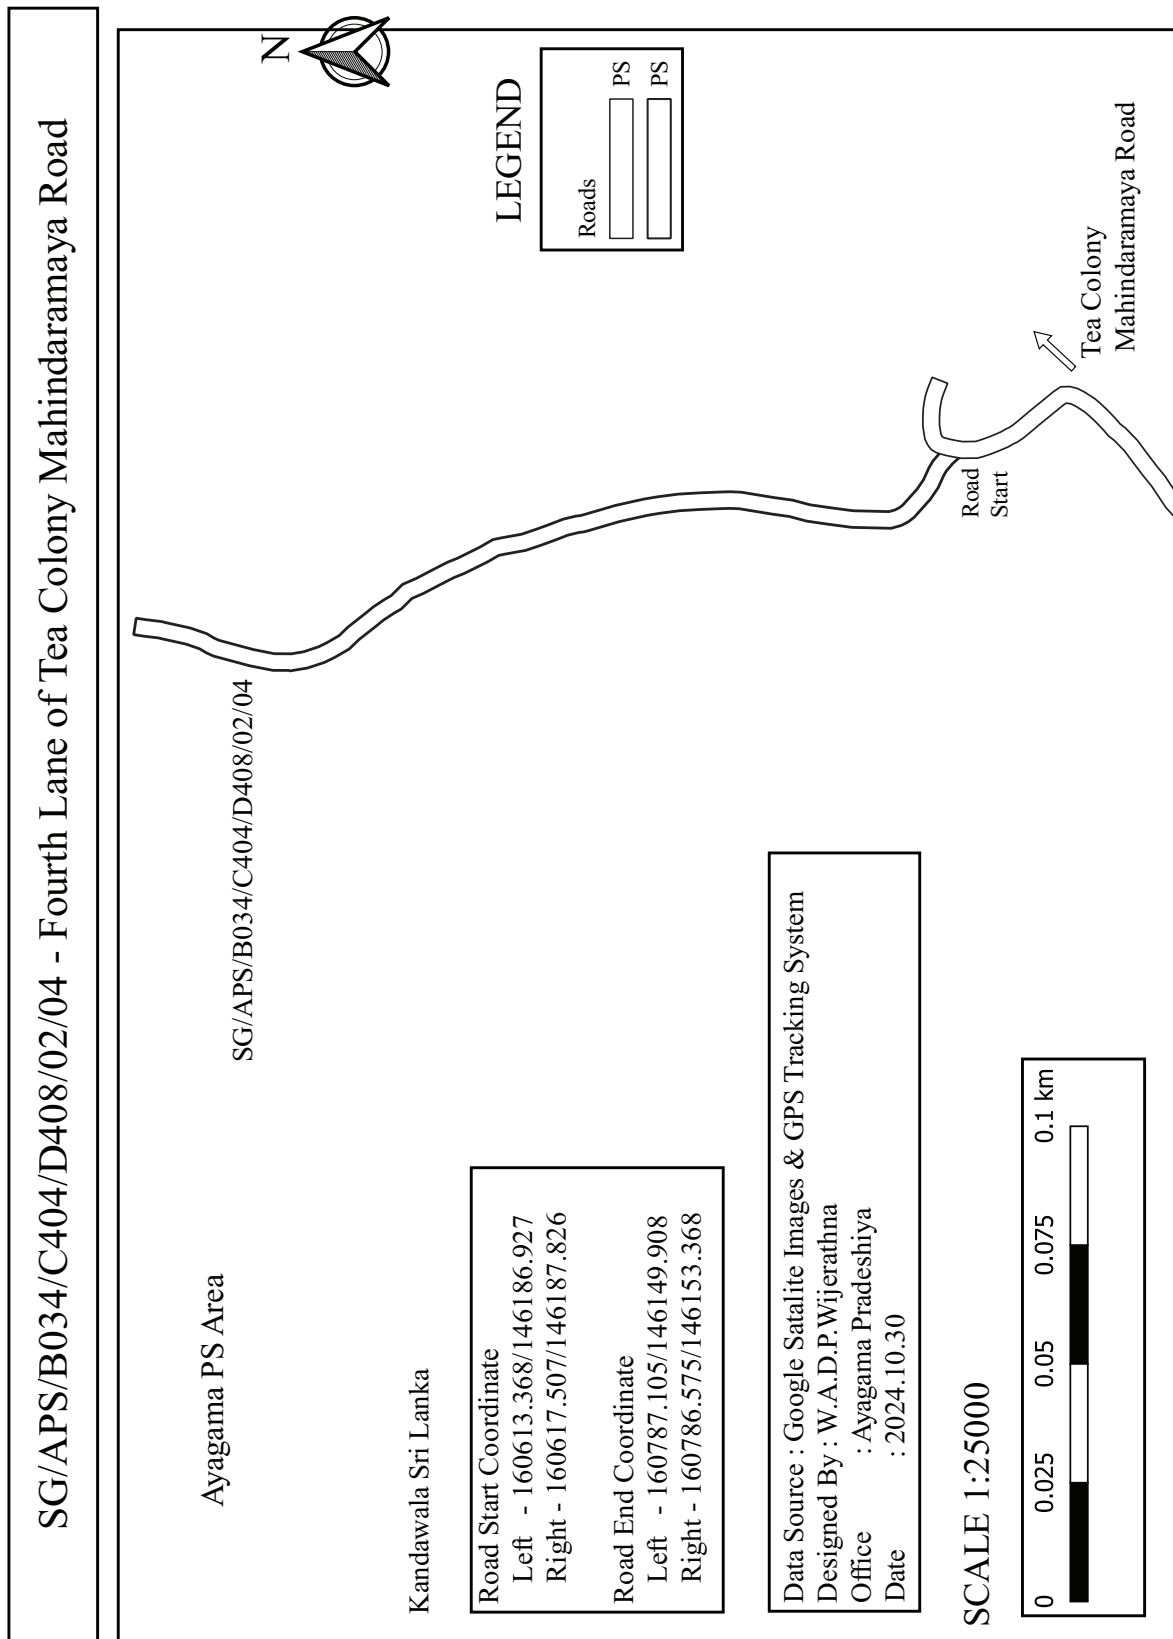


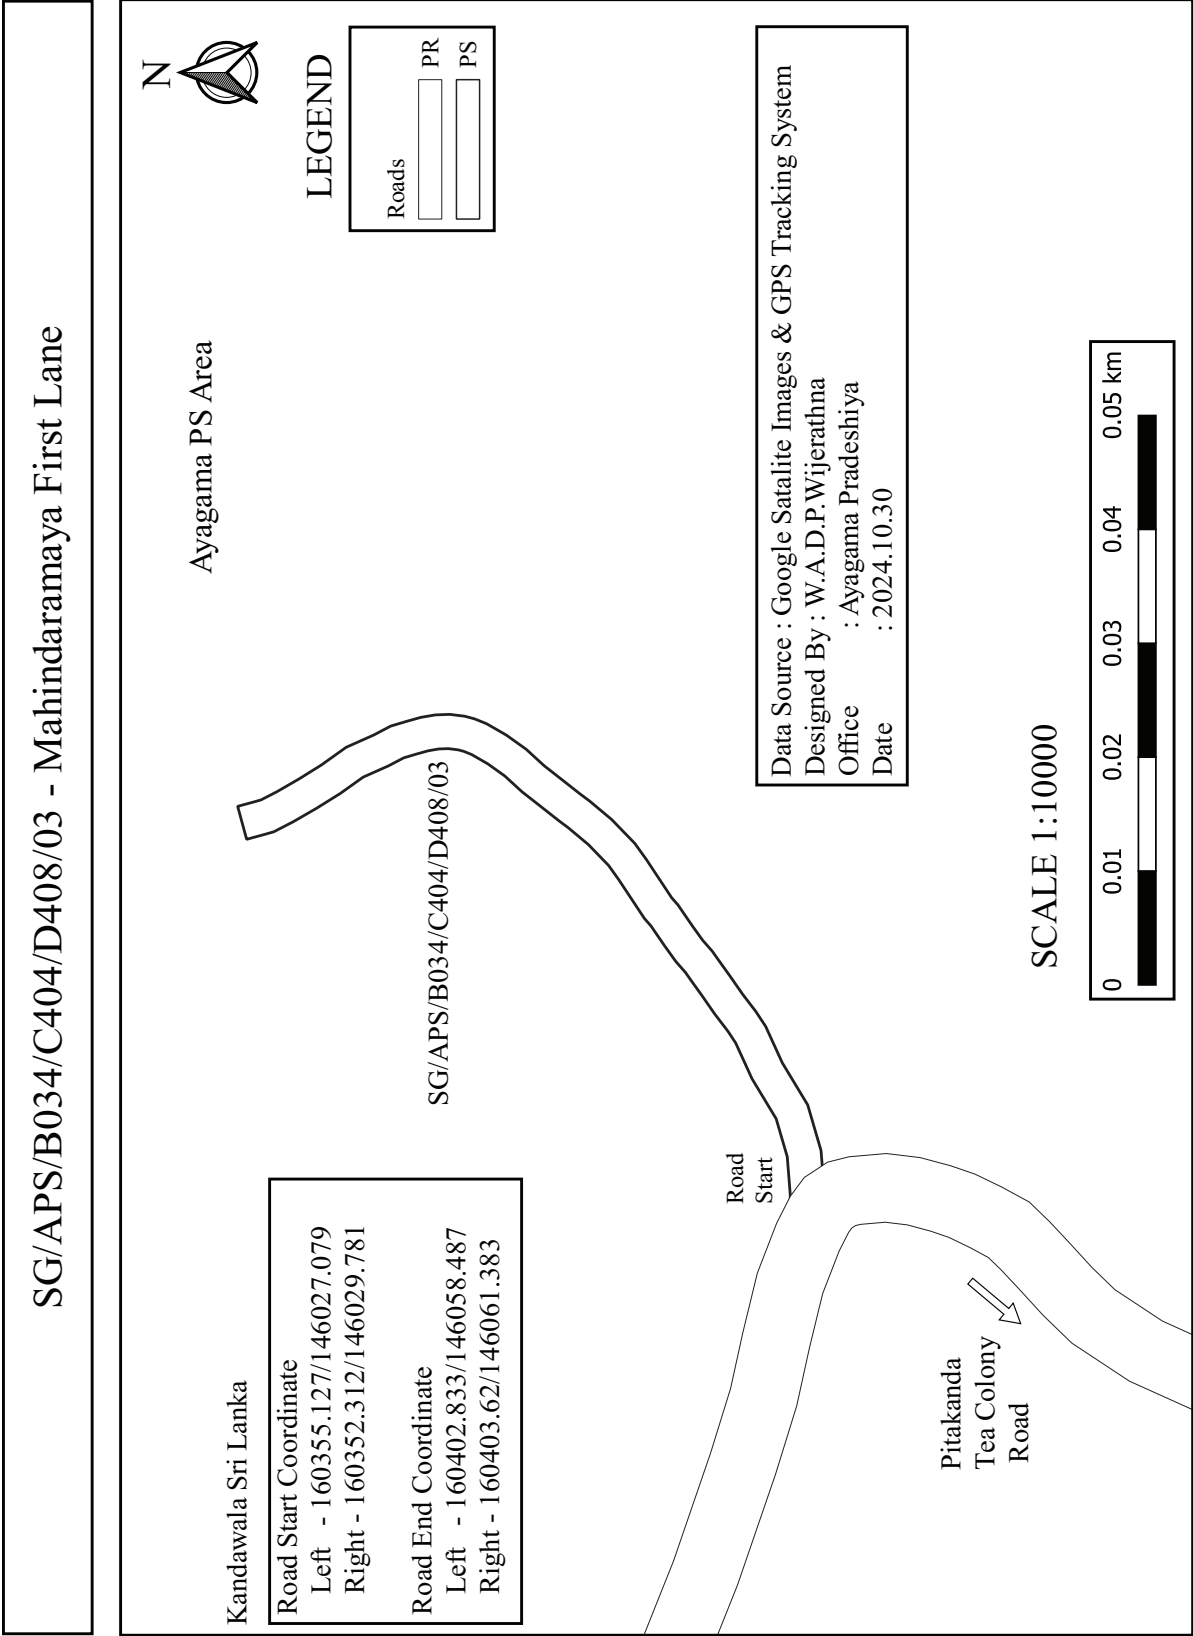




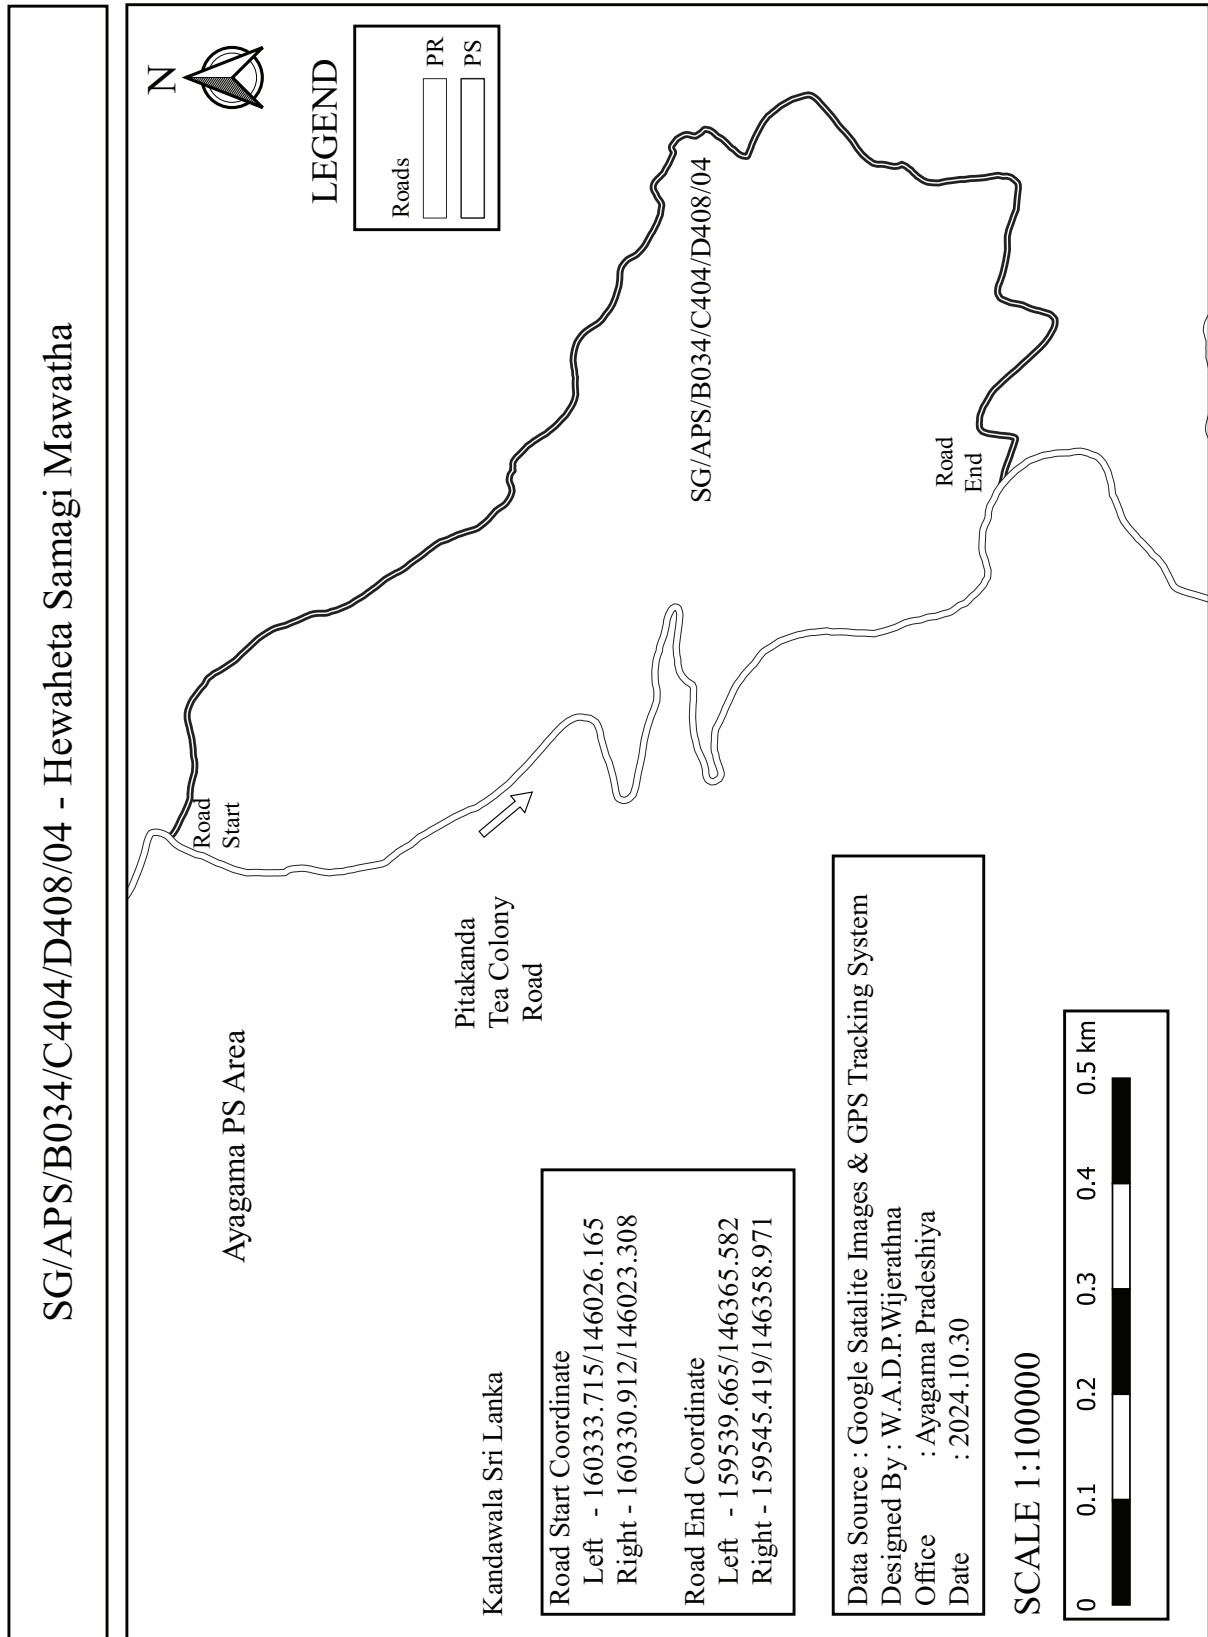


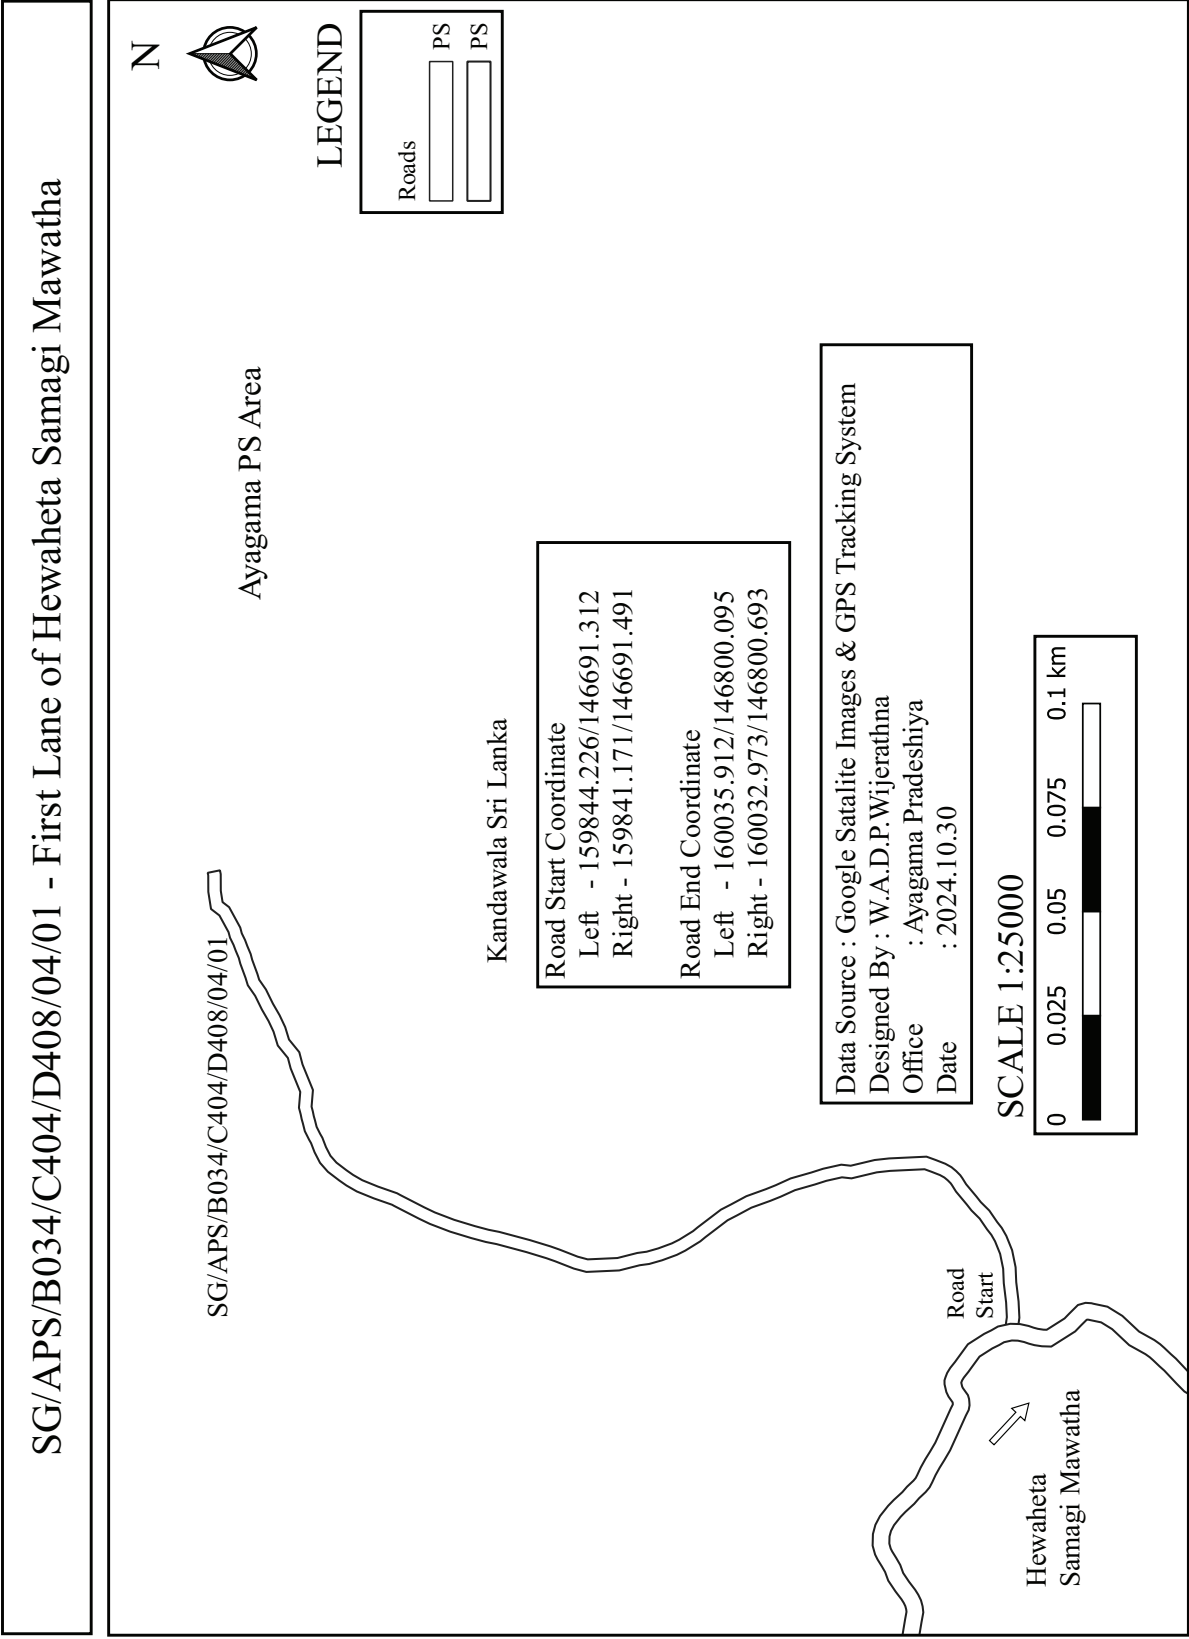


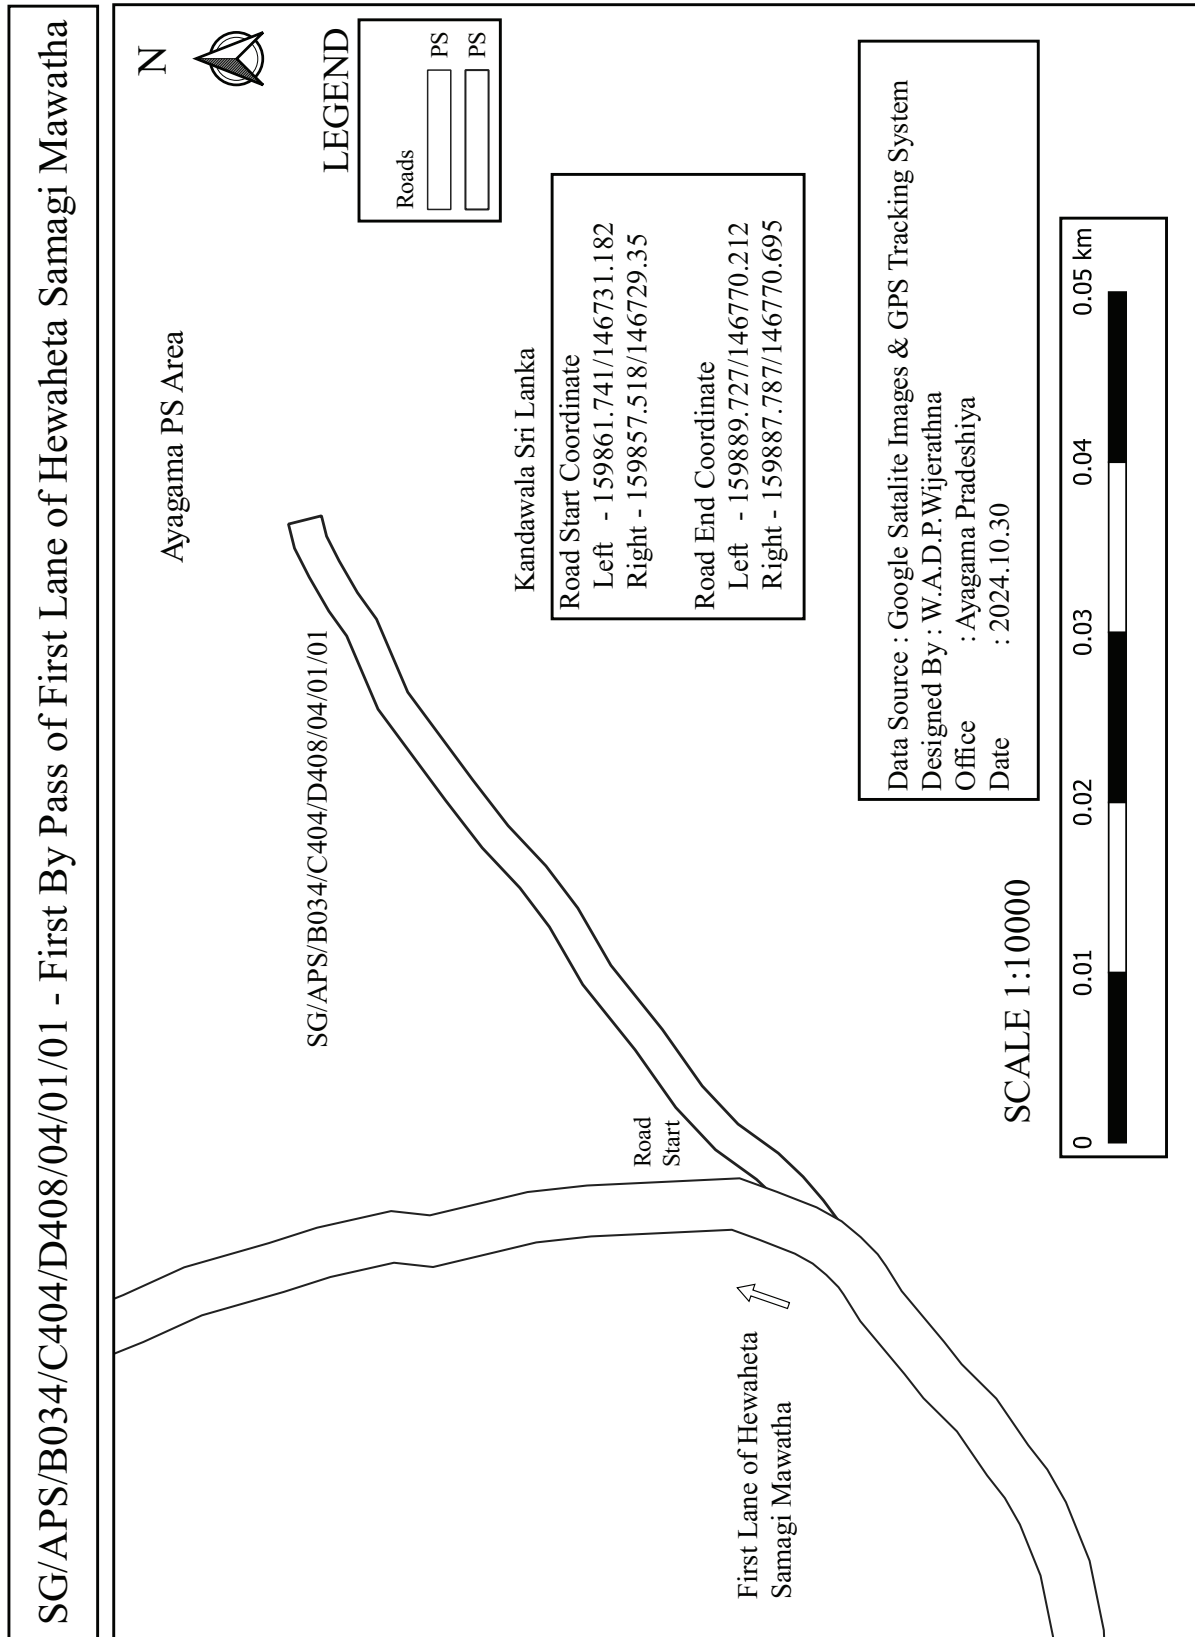


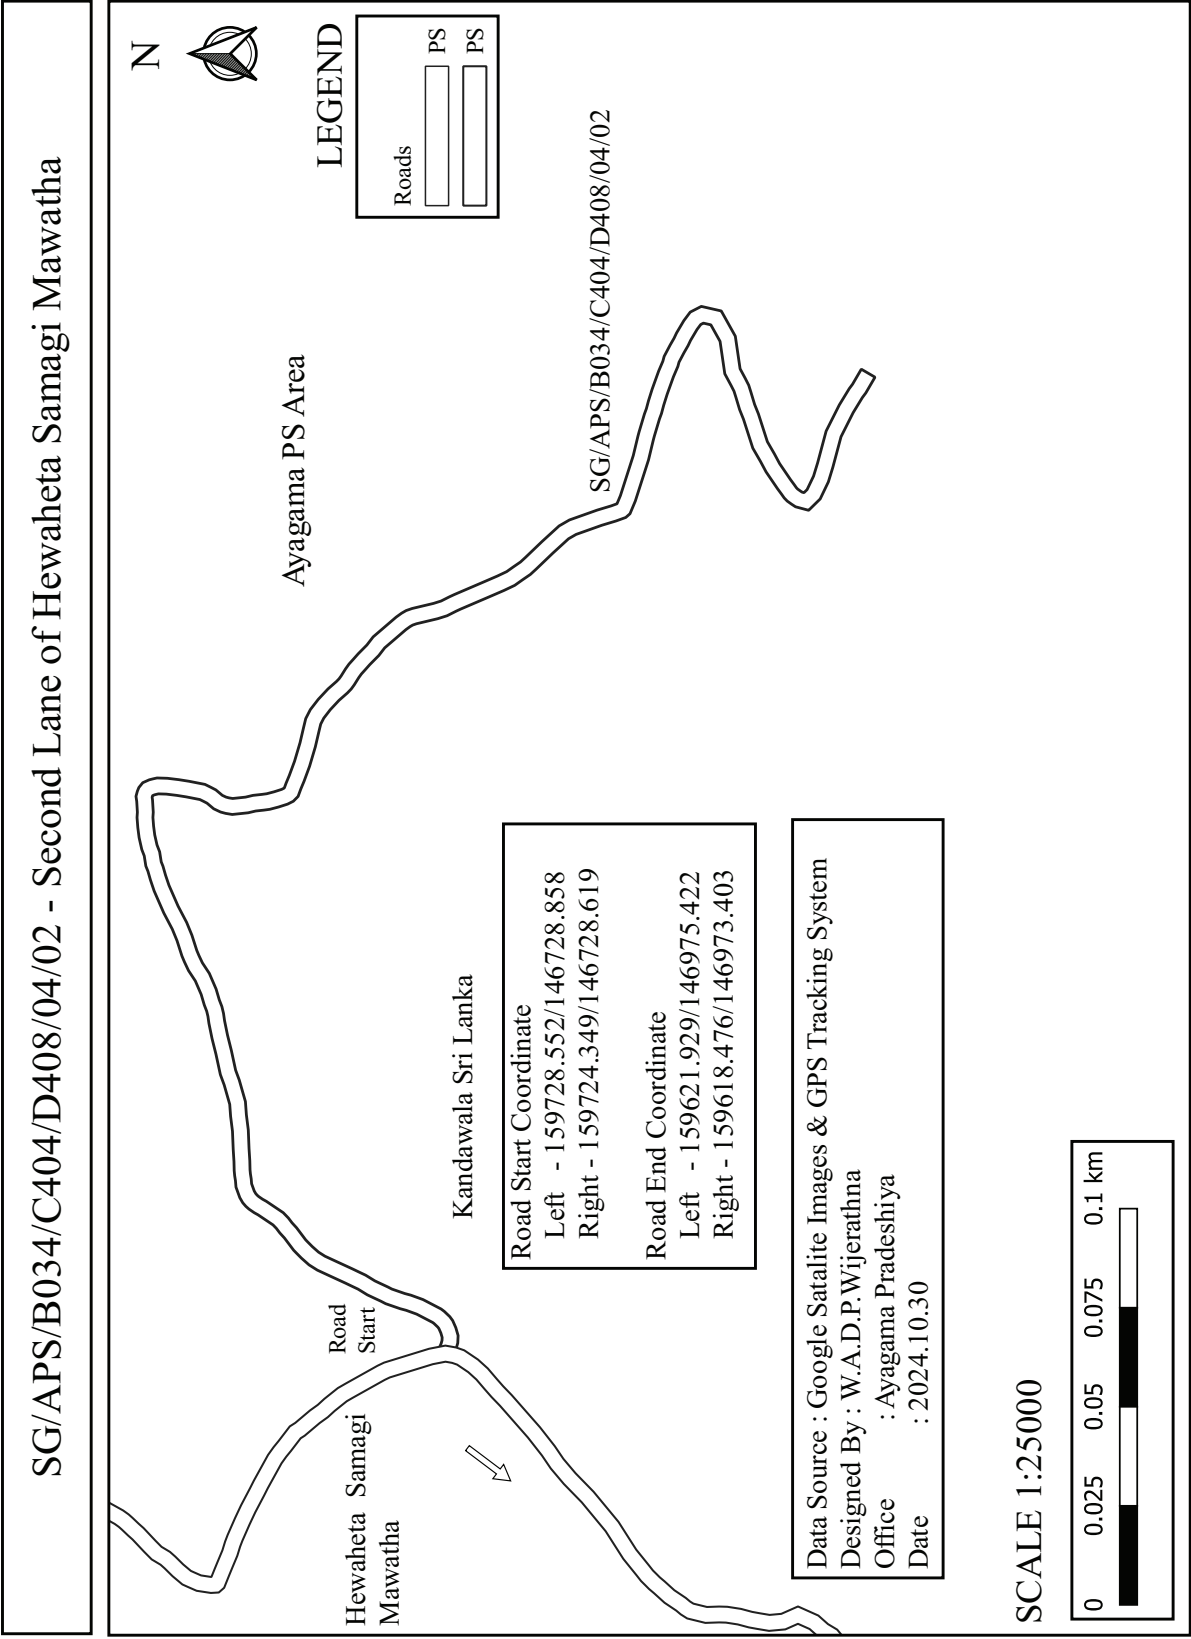


SG/APS/B034/C404/D408/04/02/01 - Footpath - First By Pass Way of Second Lane of Hewaheta  
Samagi Mawatha

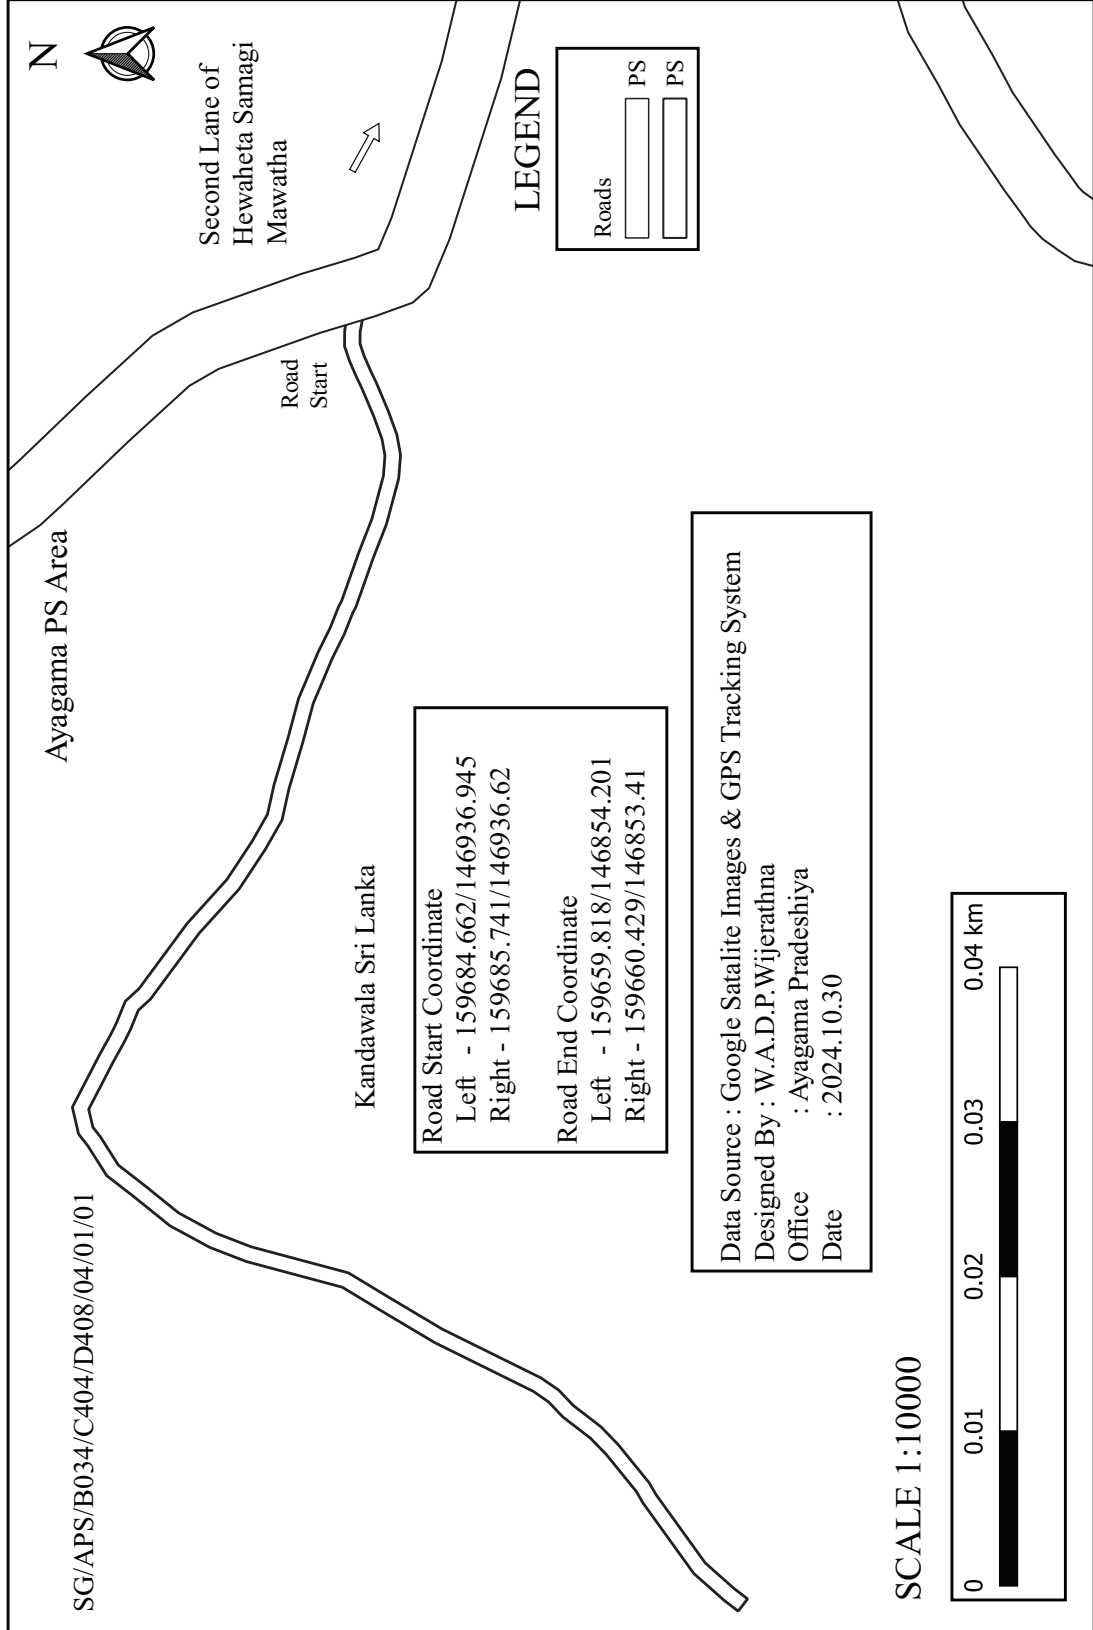

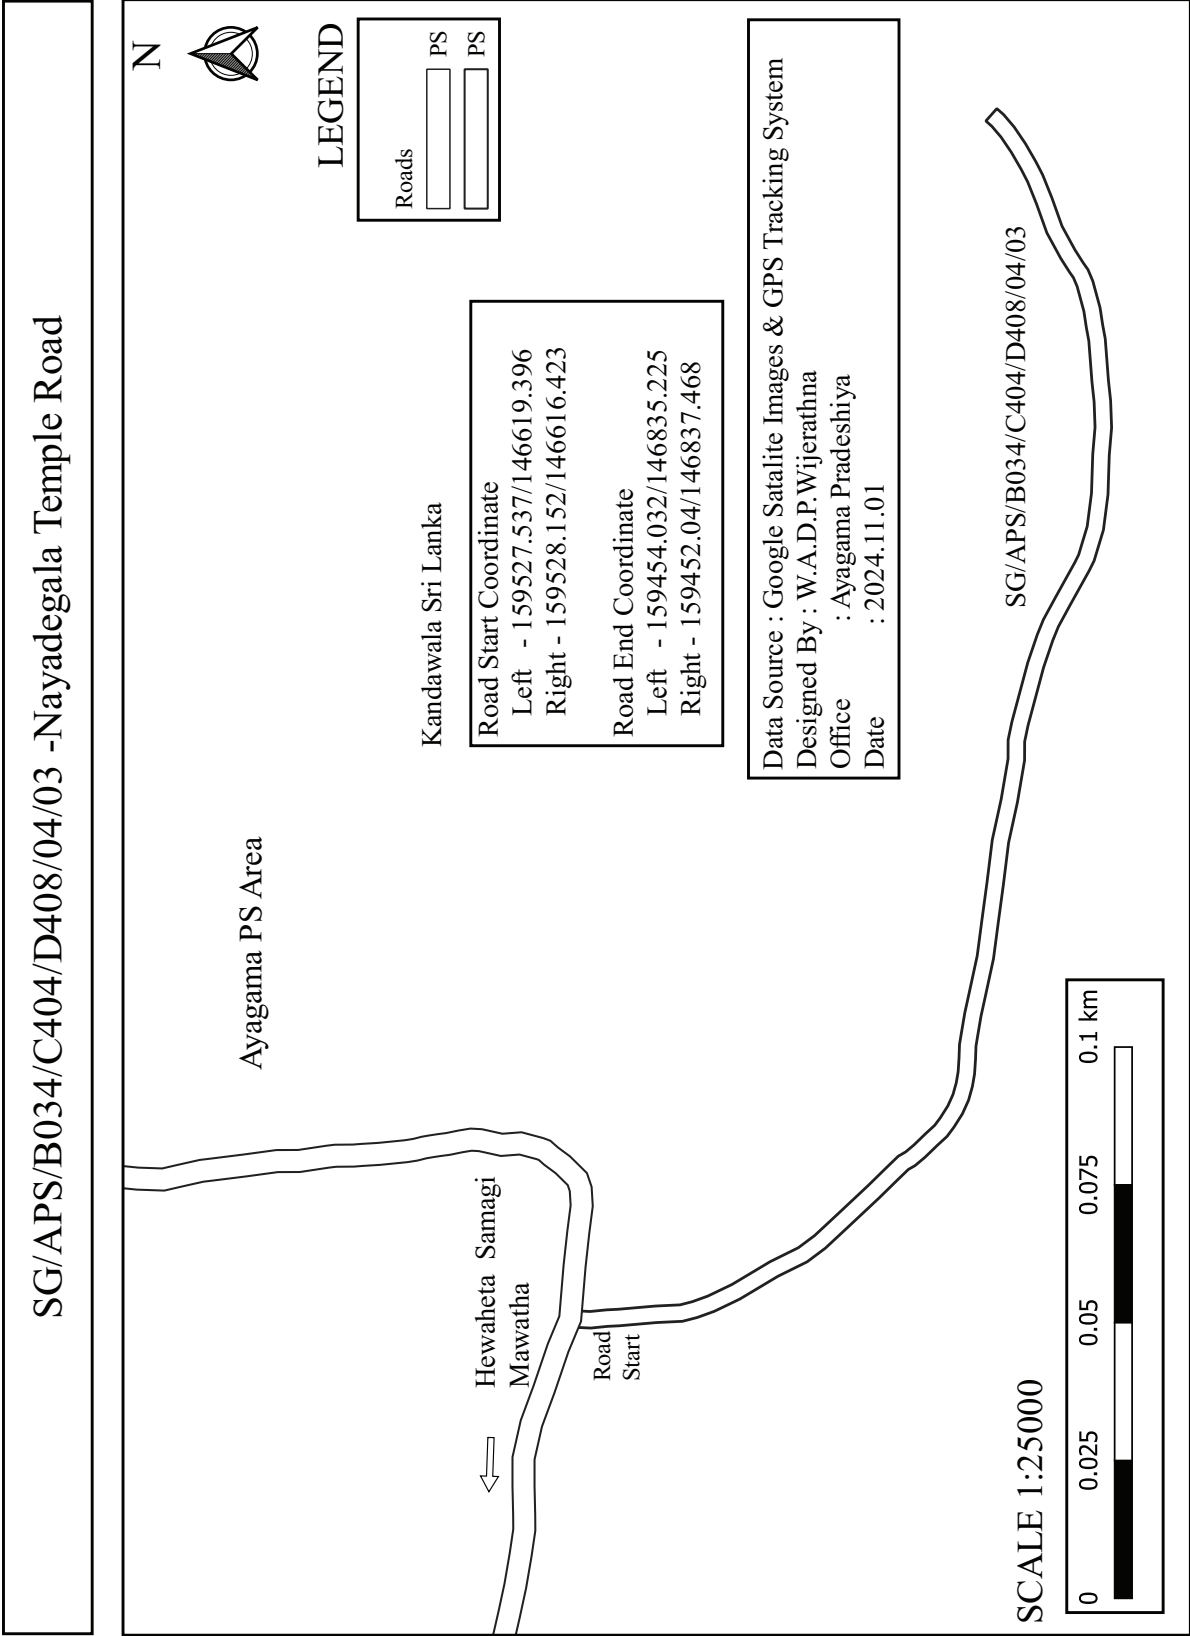


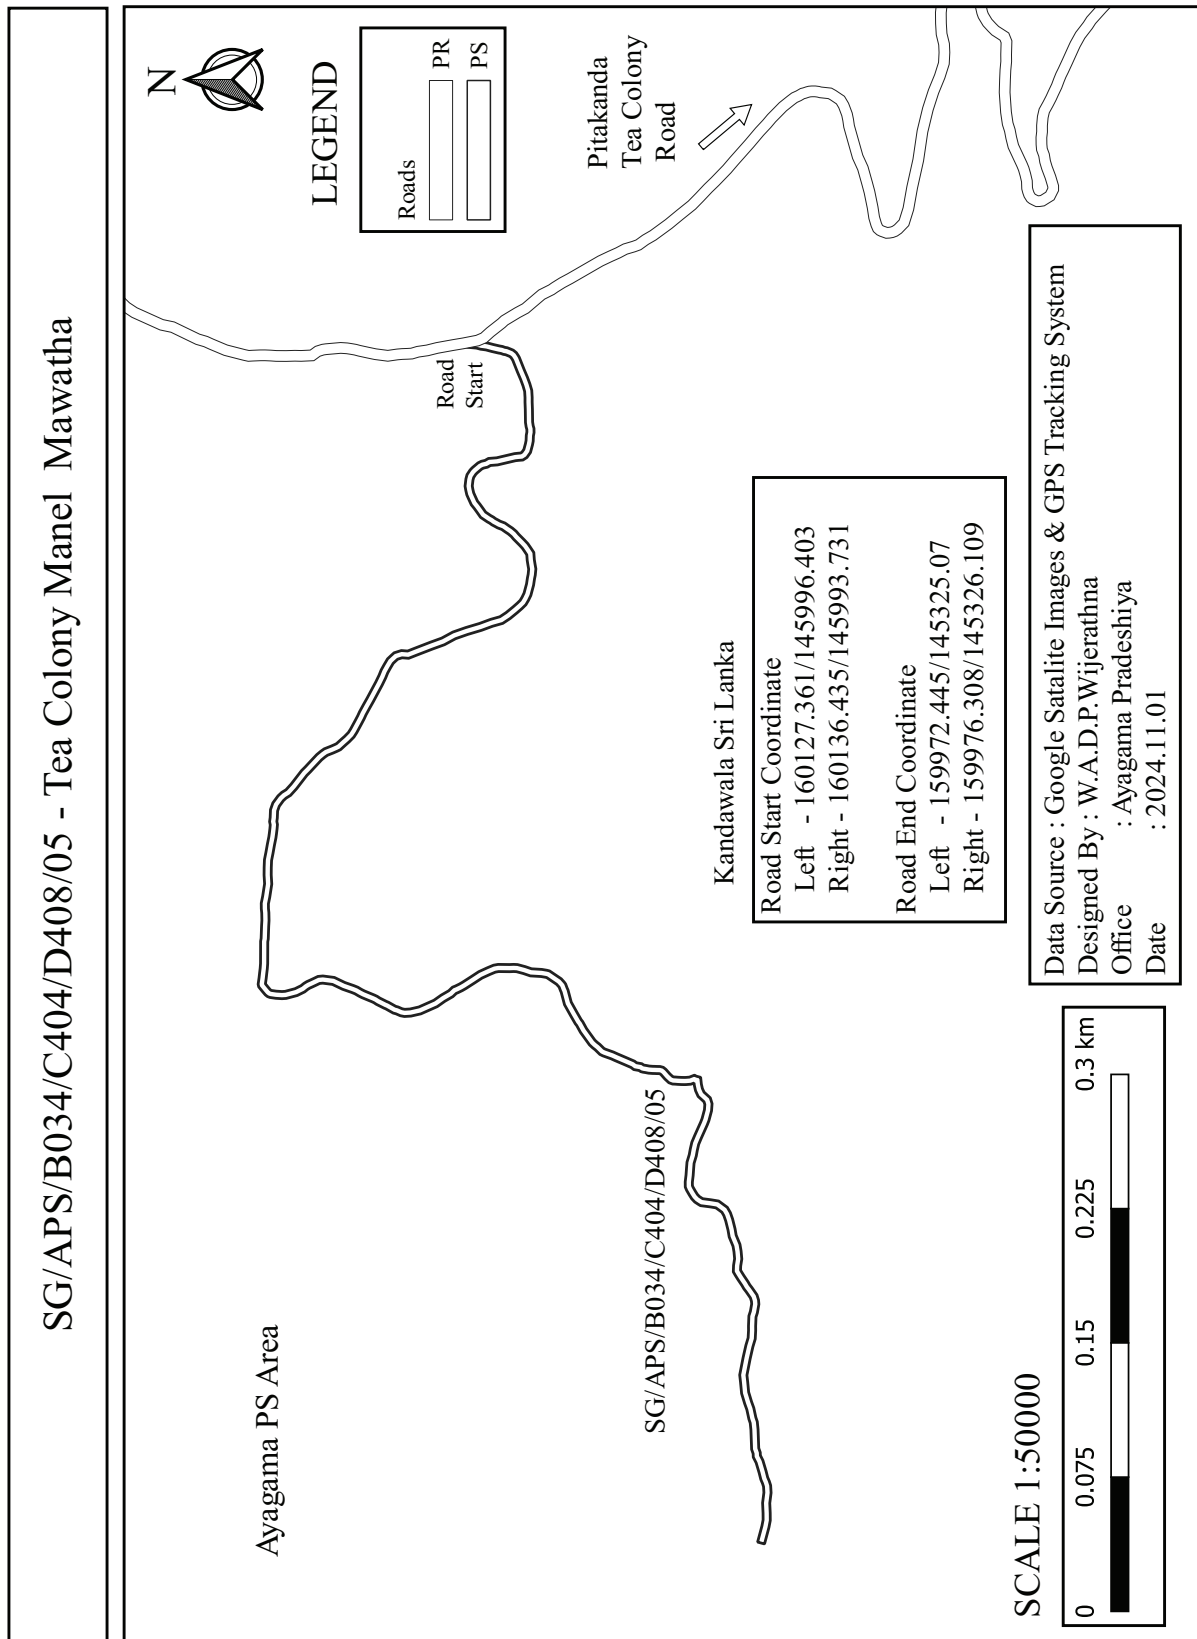


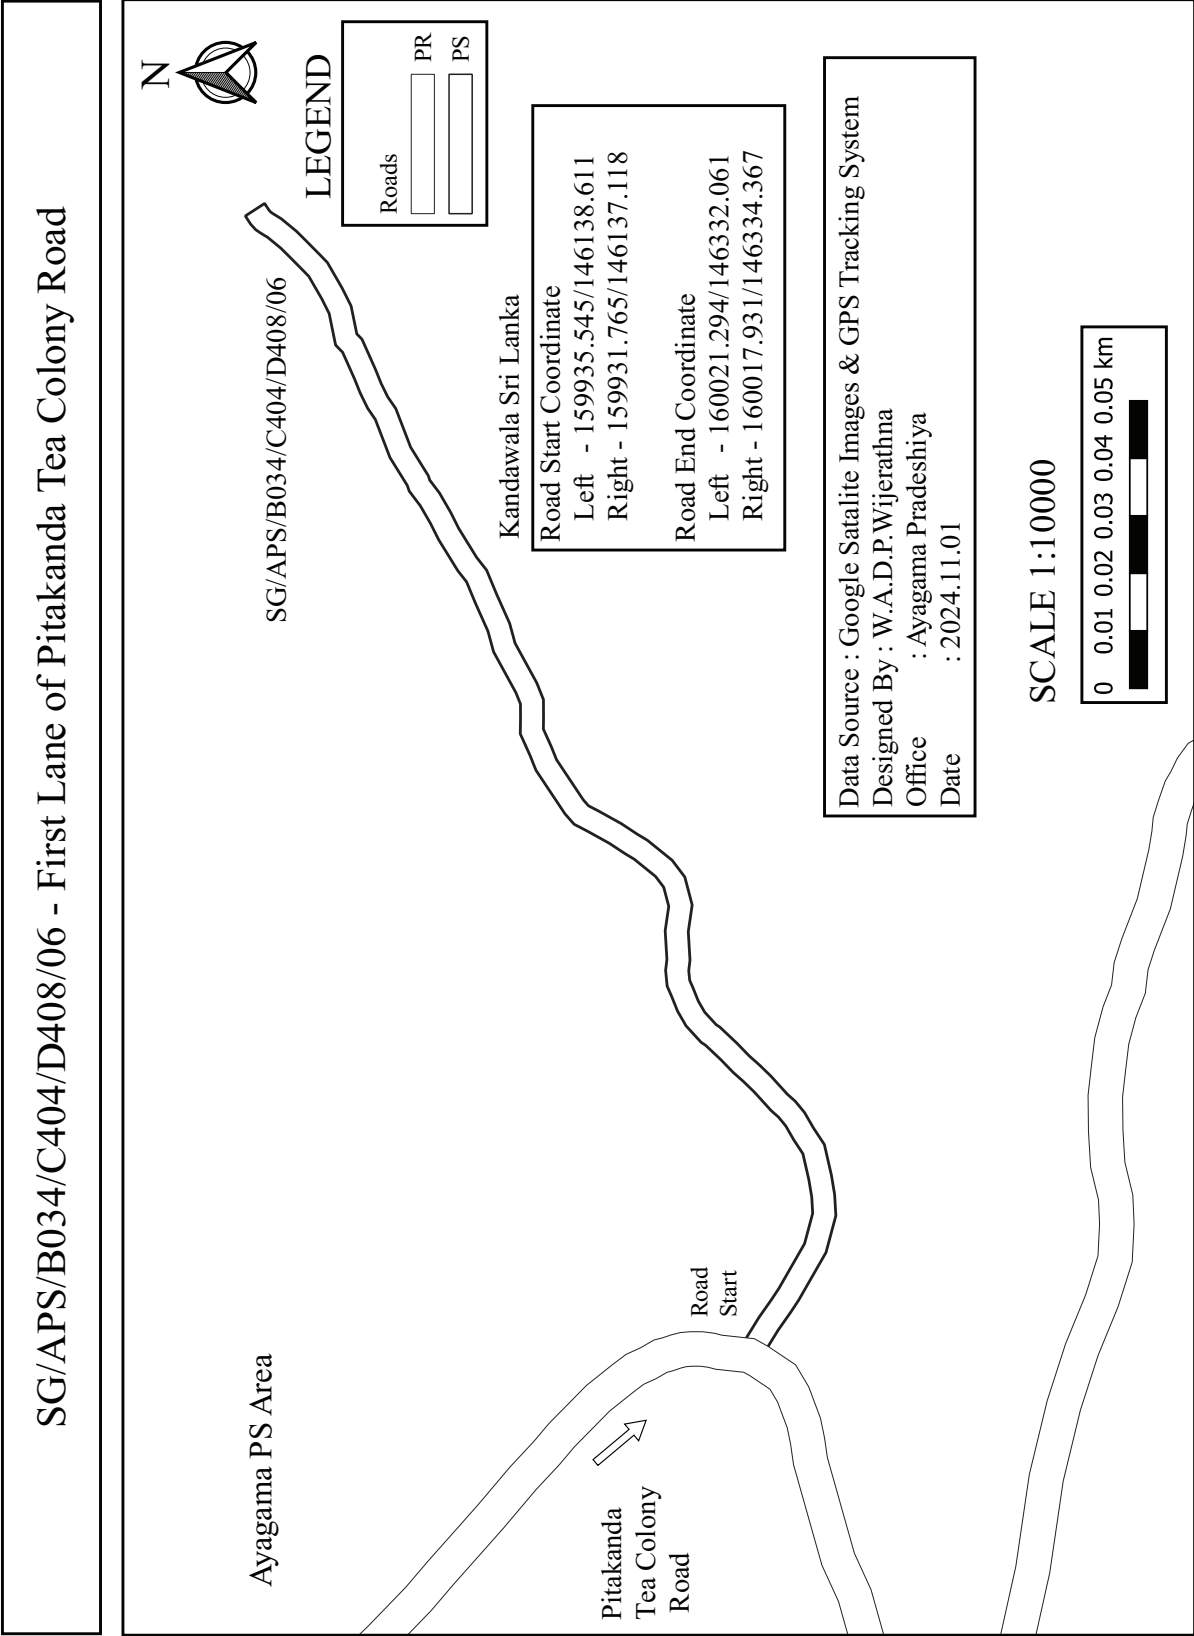






SG/APS/B034/C404/D408/07 - Second Lane of Pitakanda Tea Colony Road

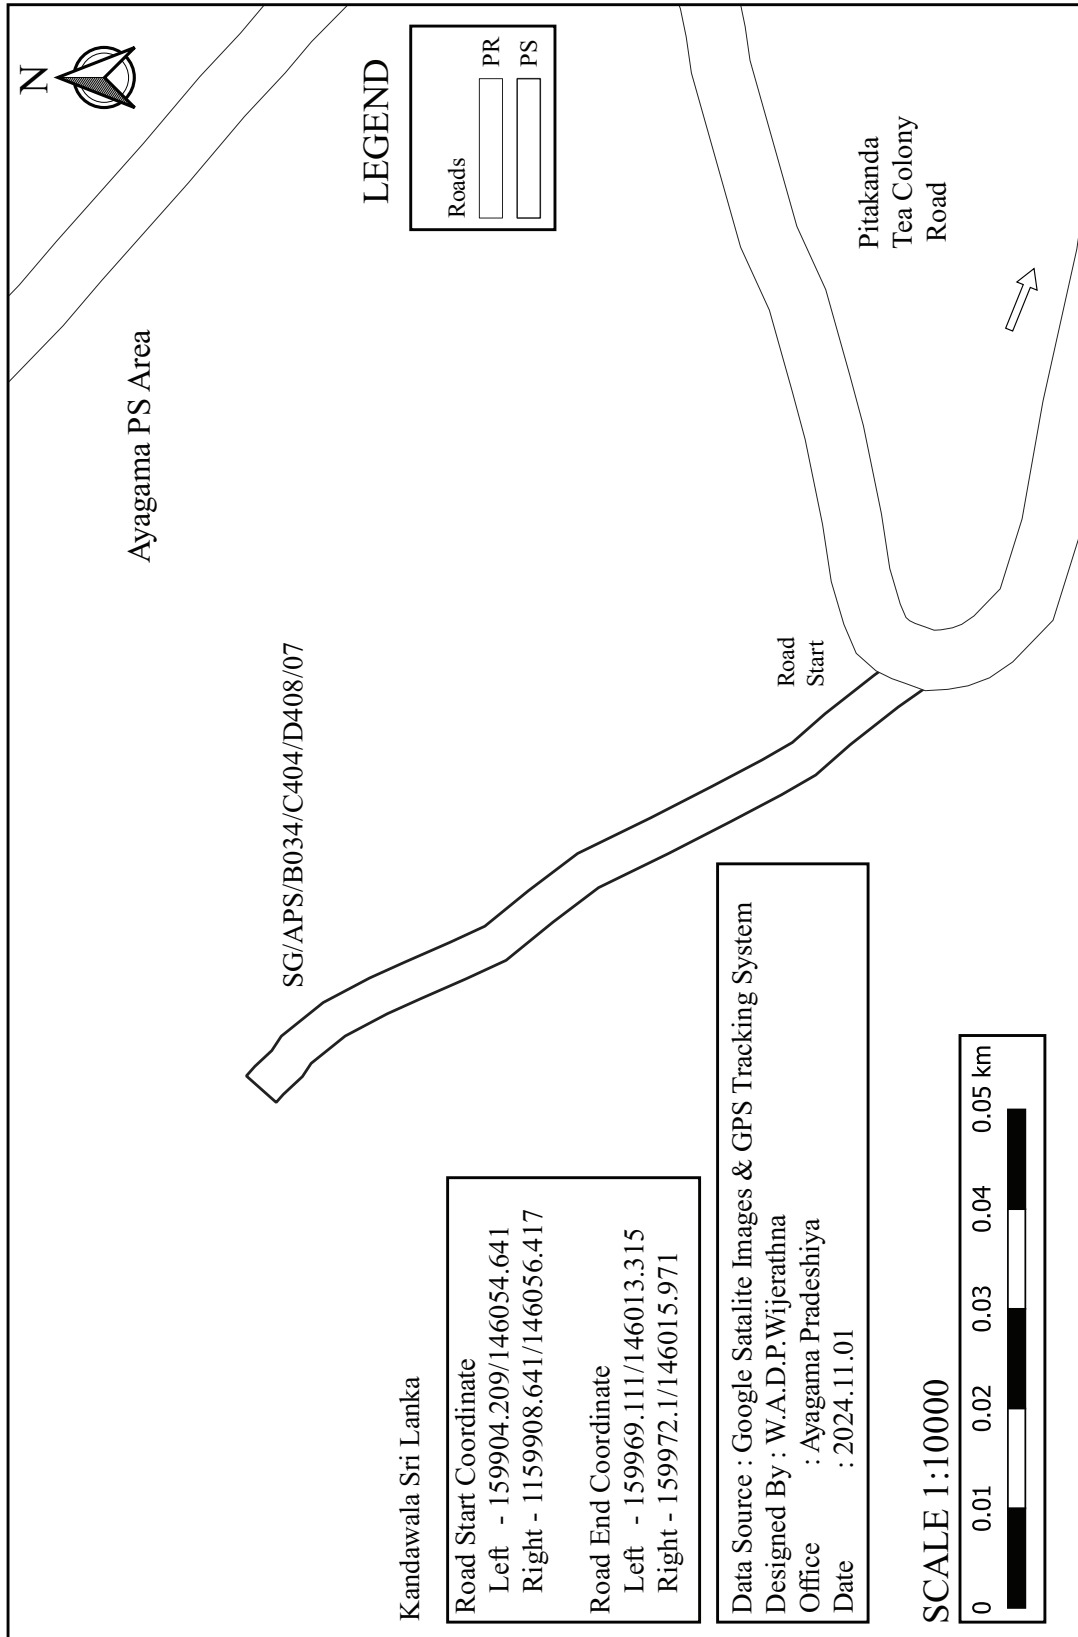


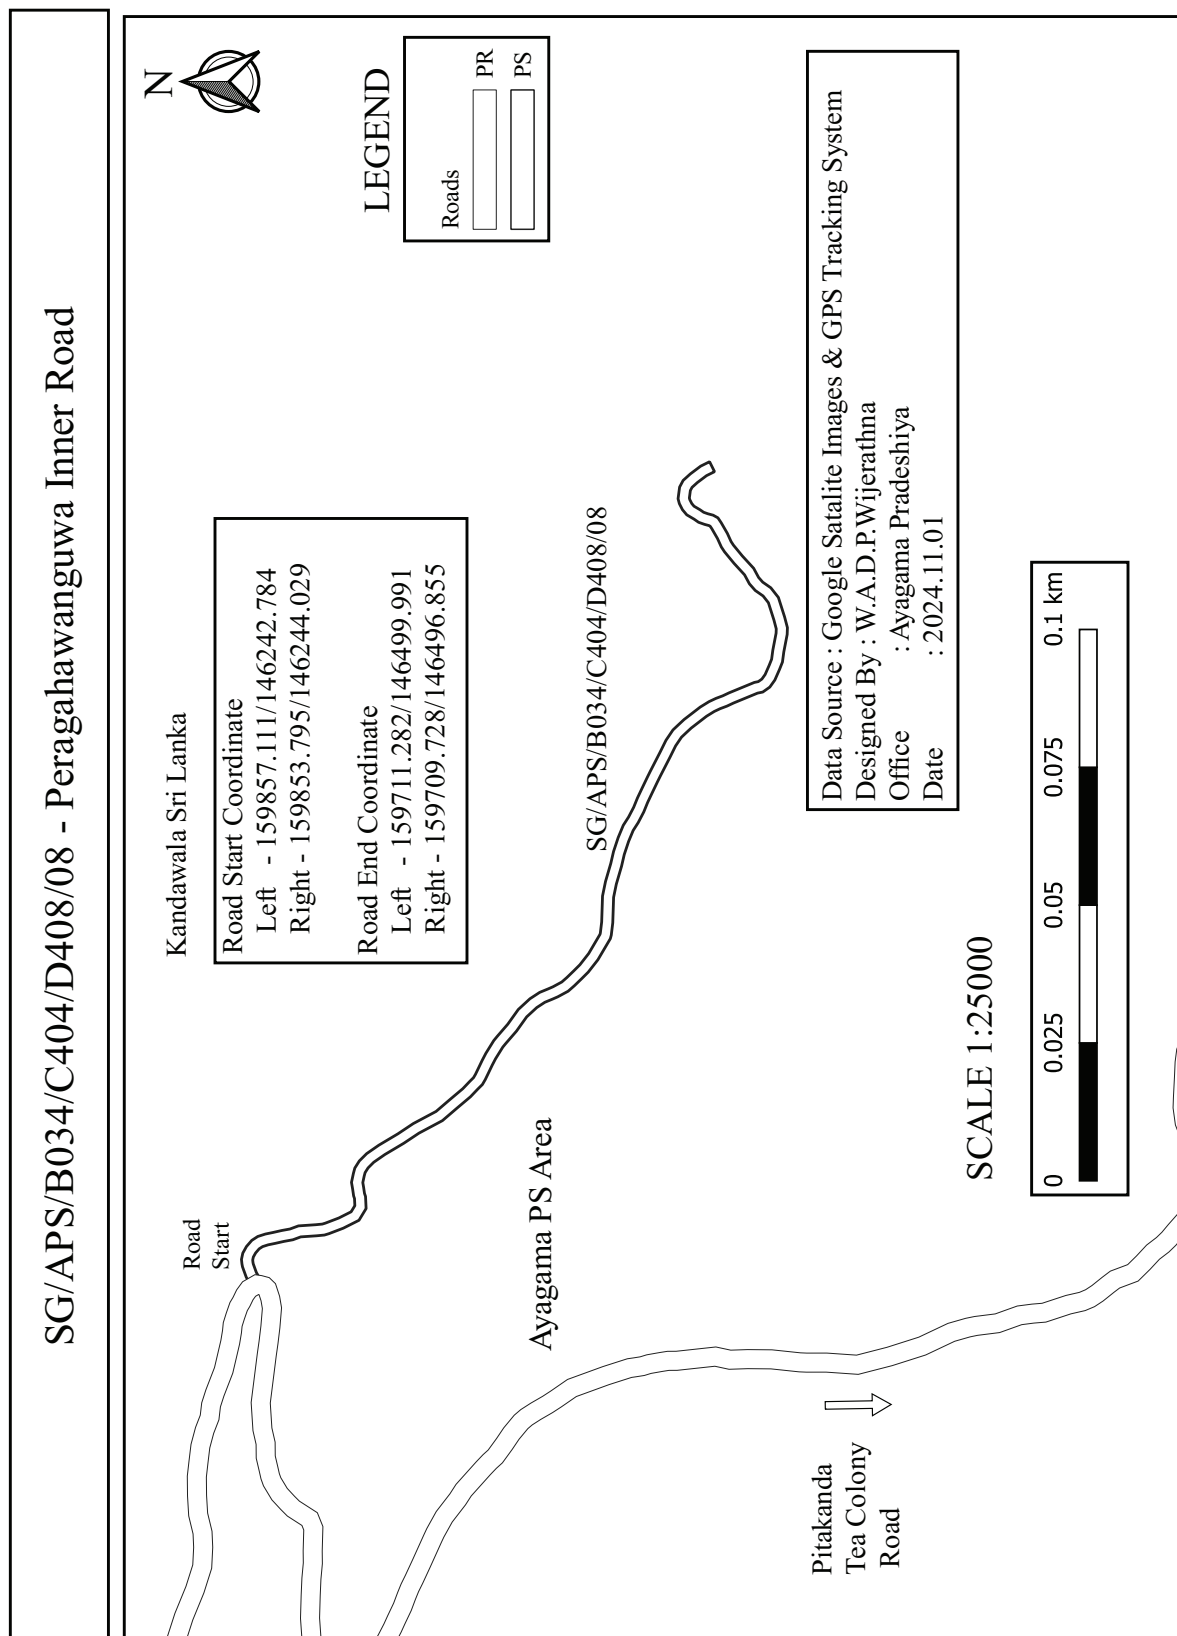


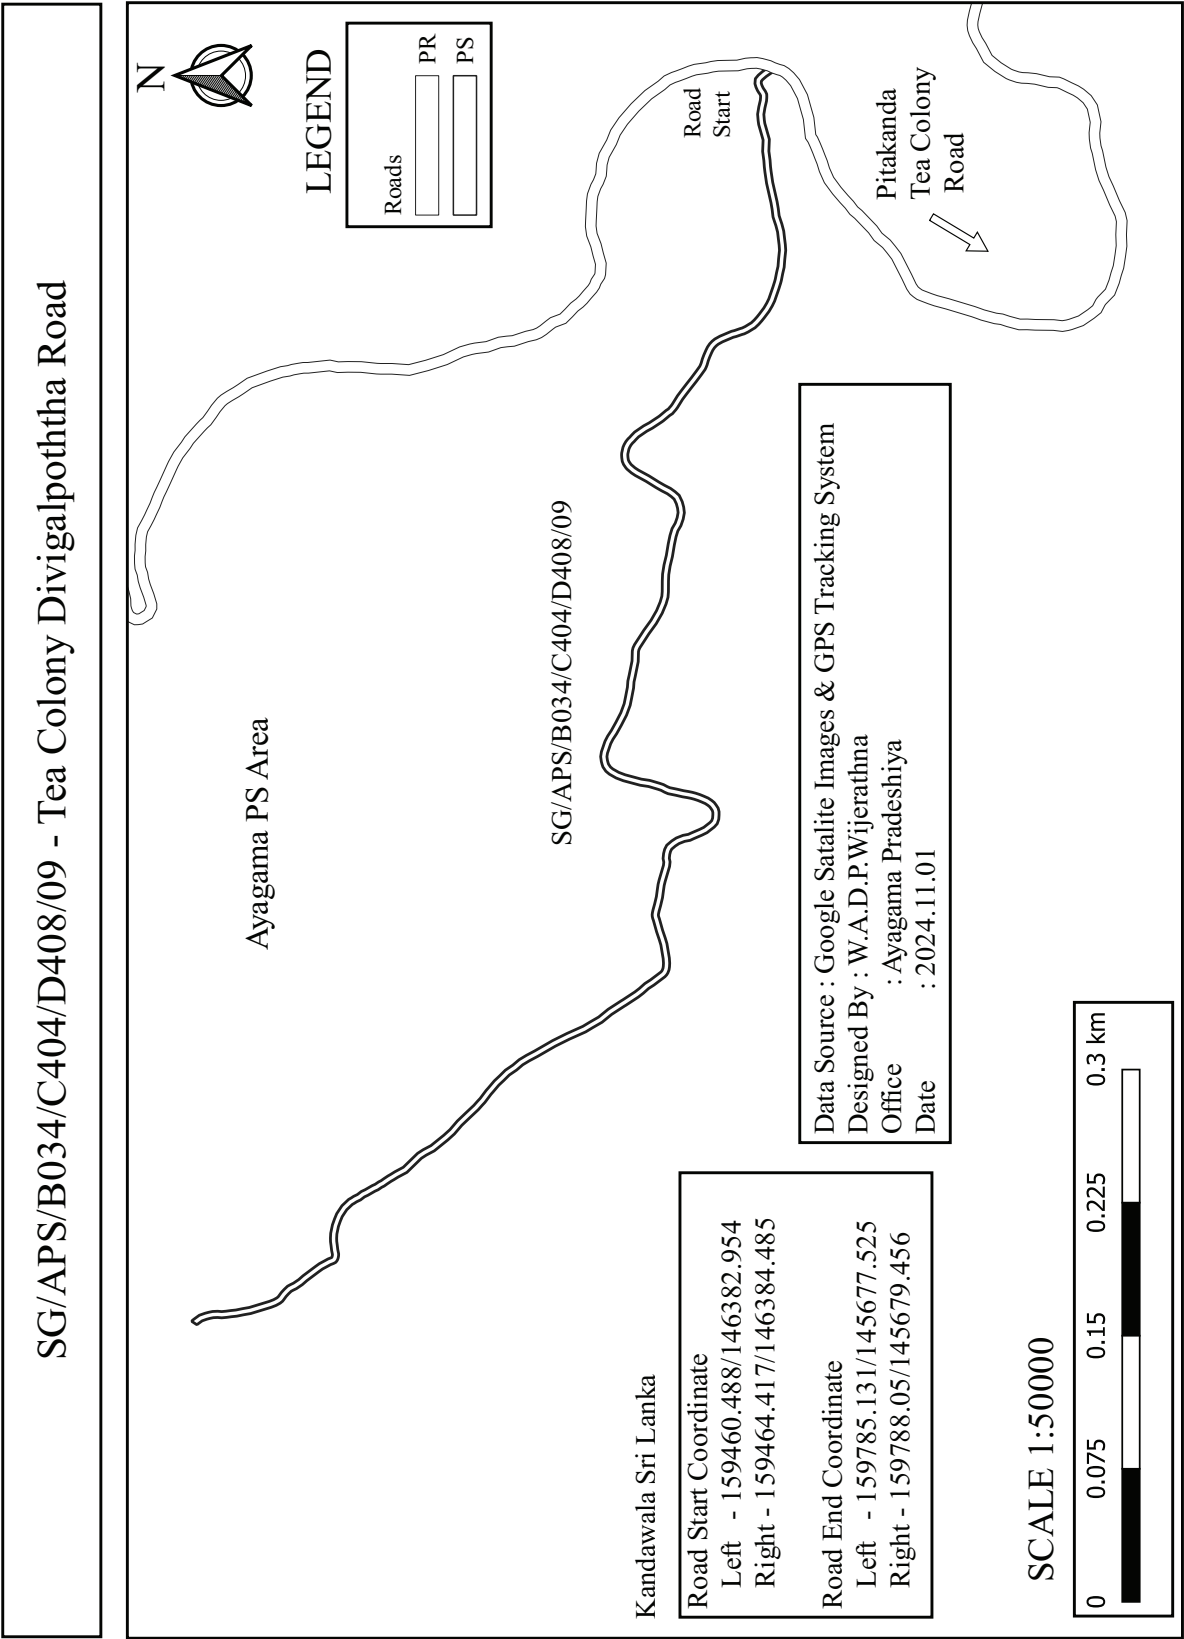


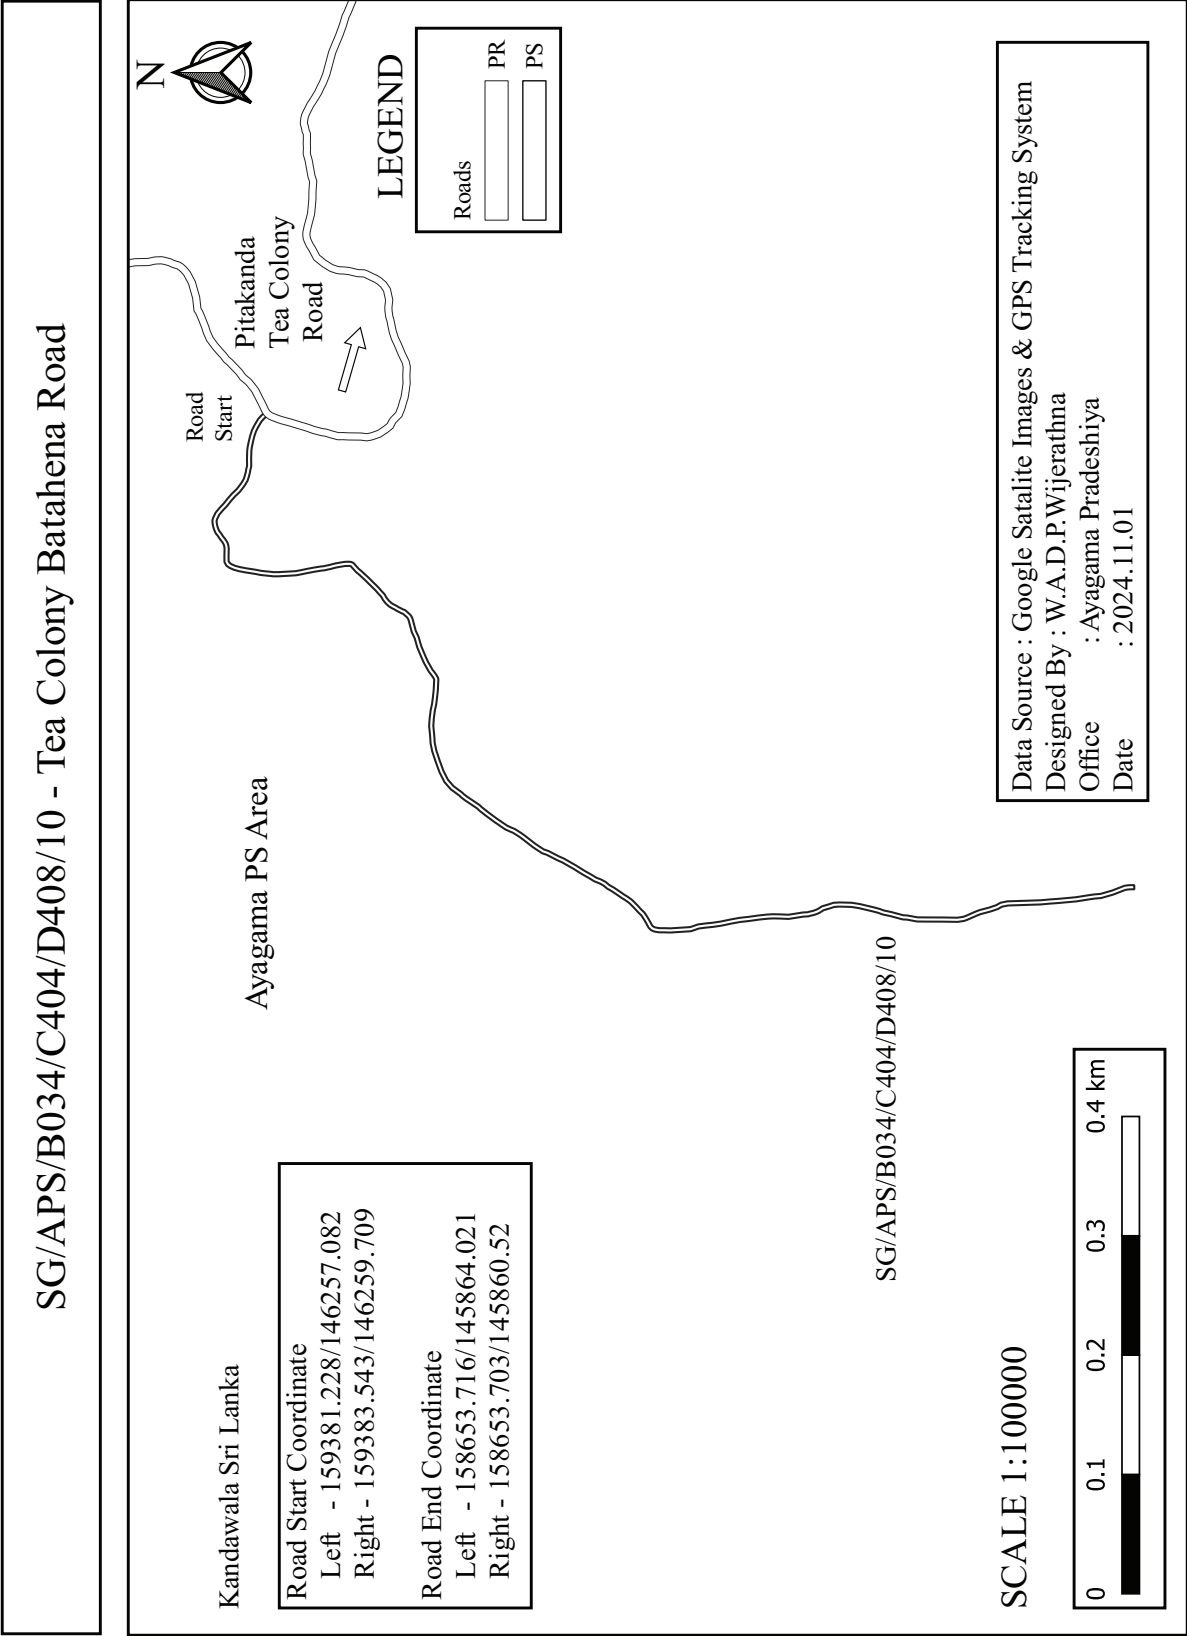

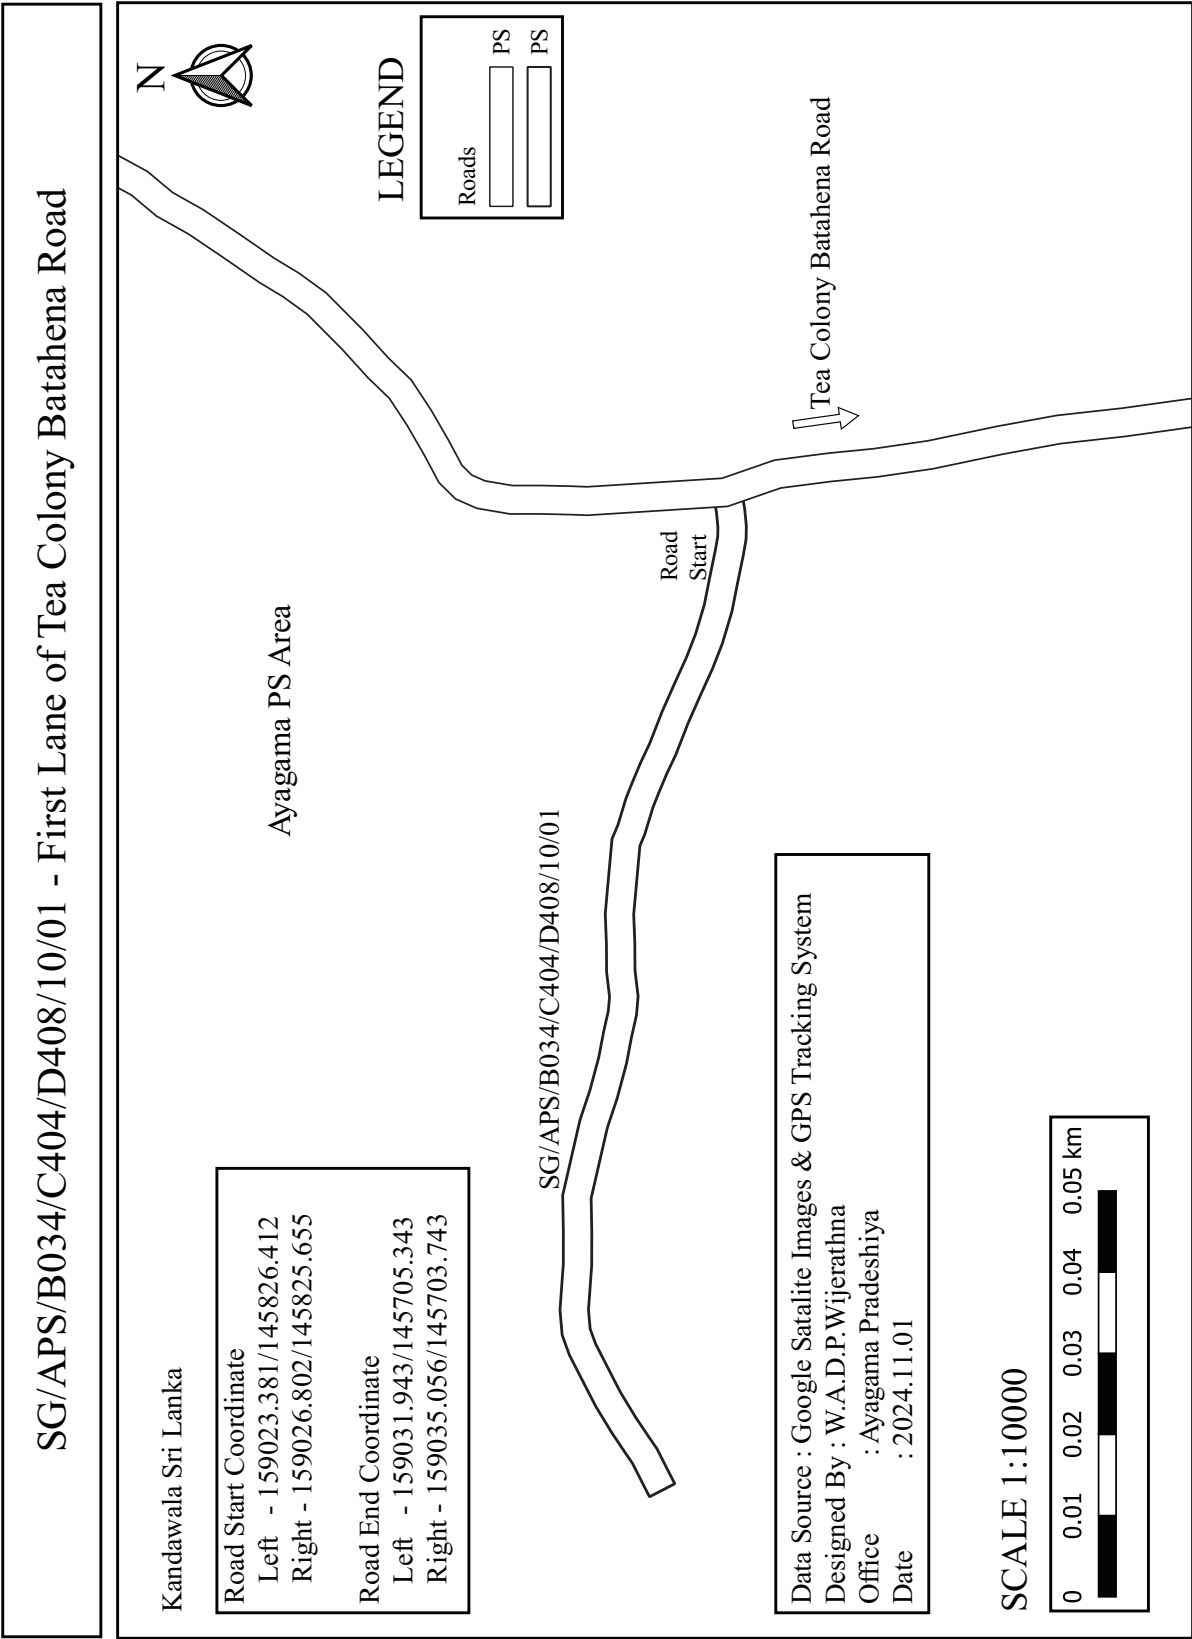


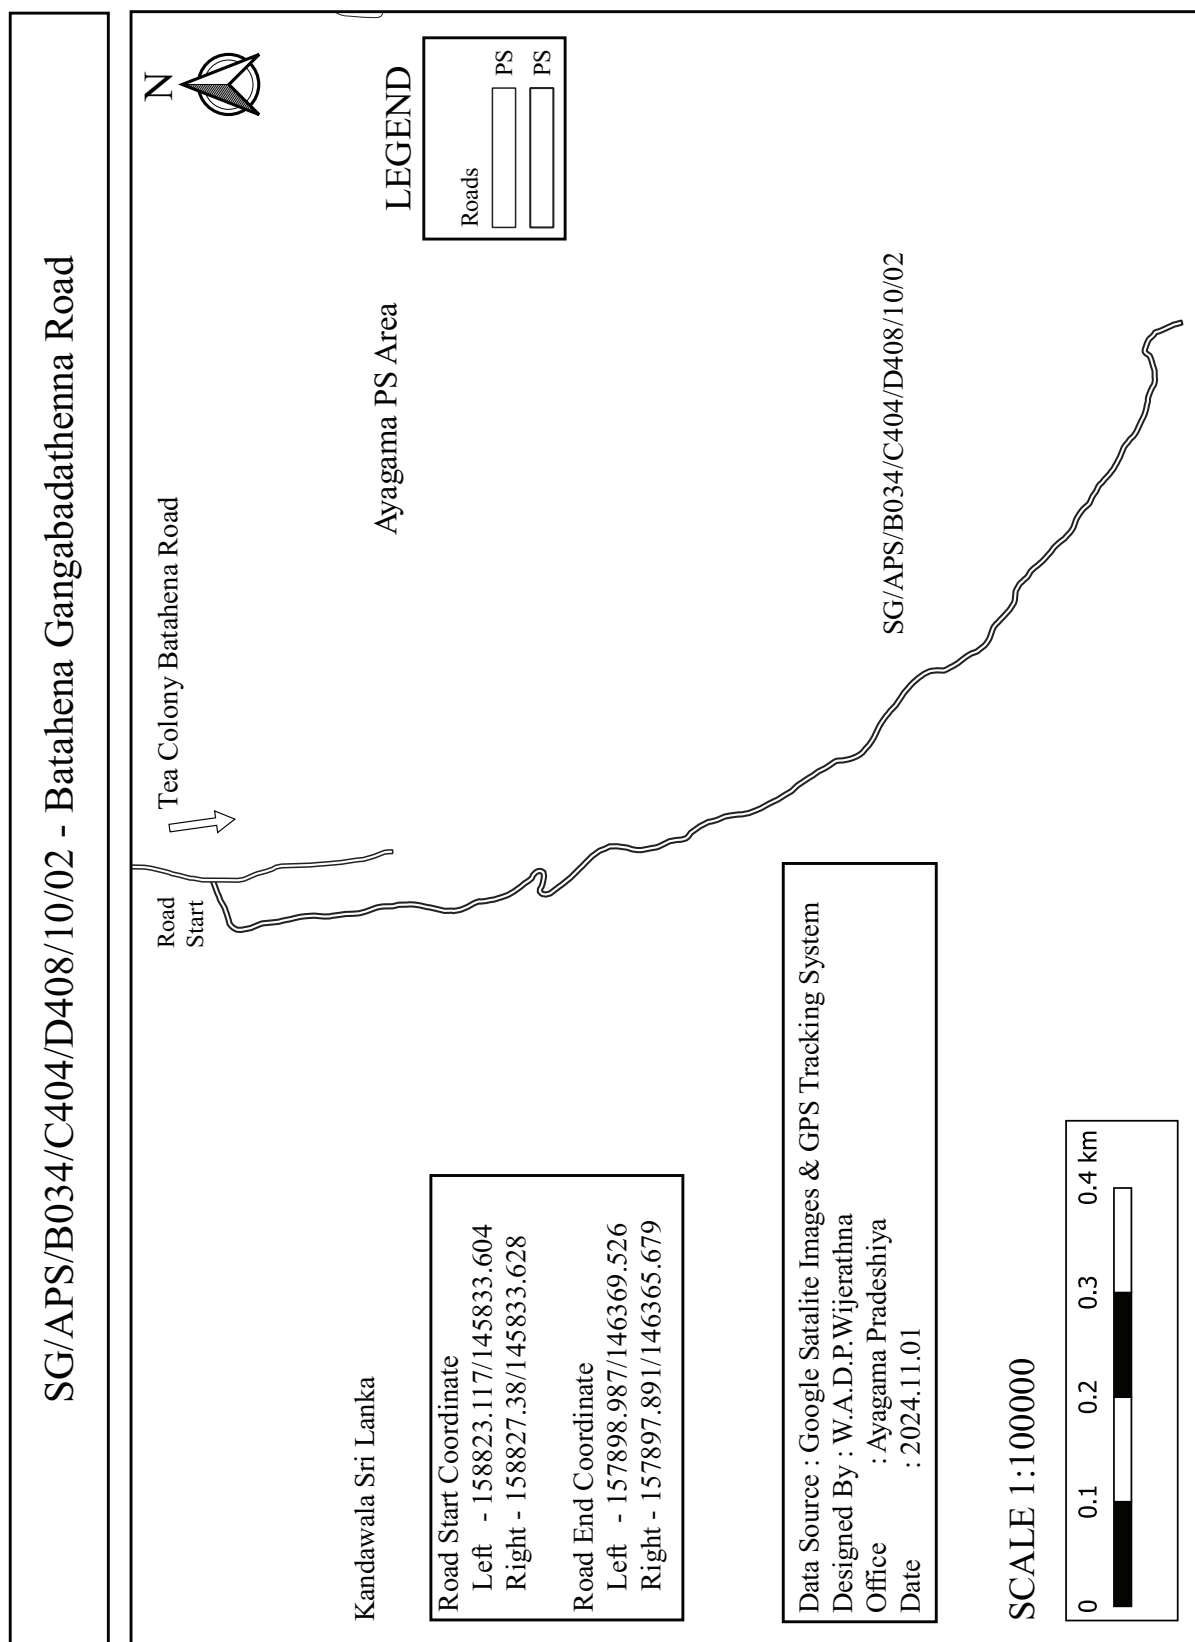


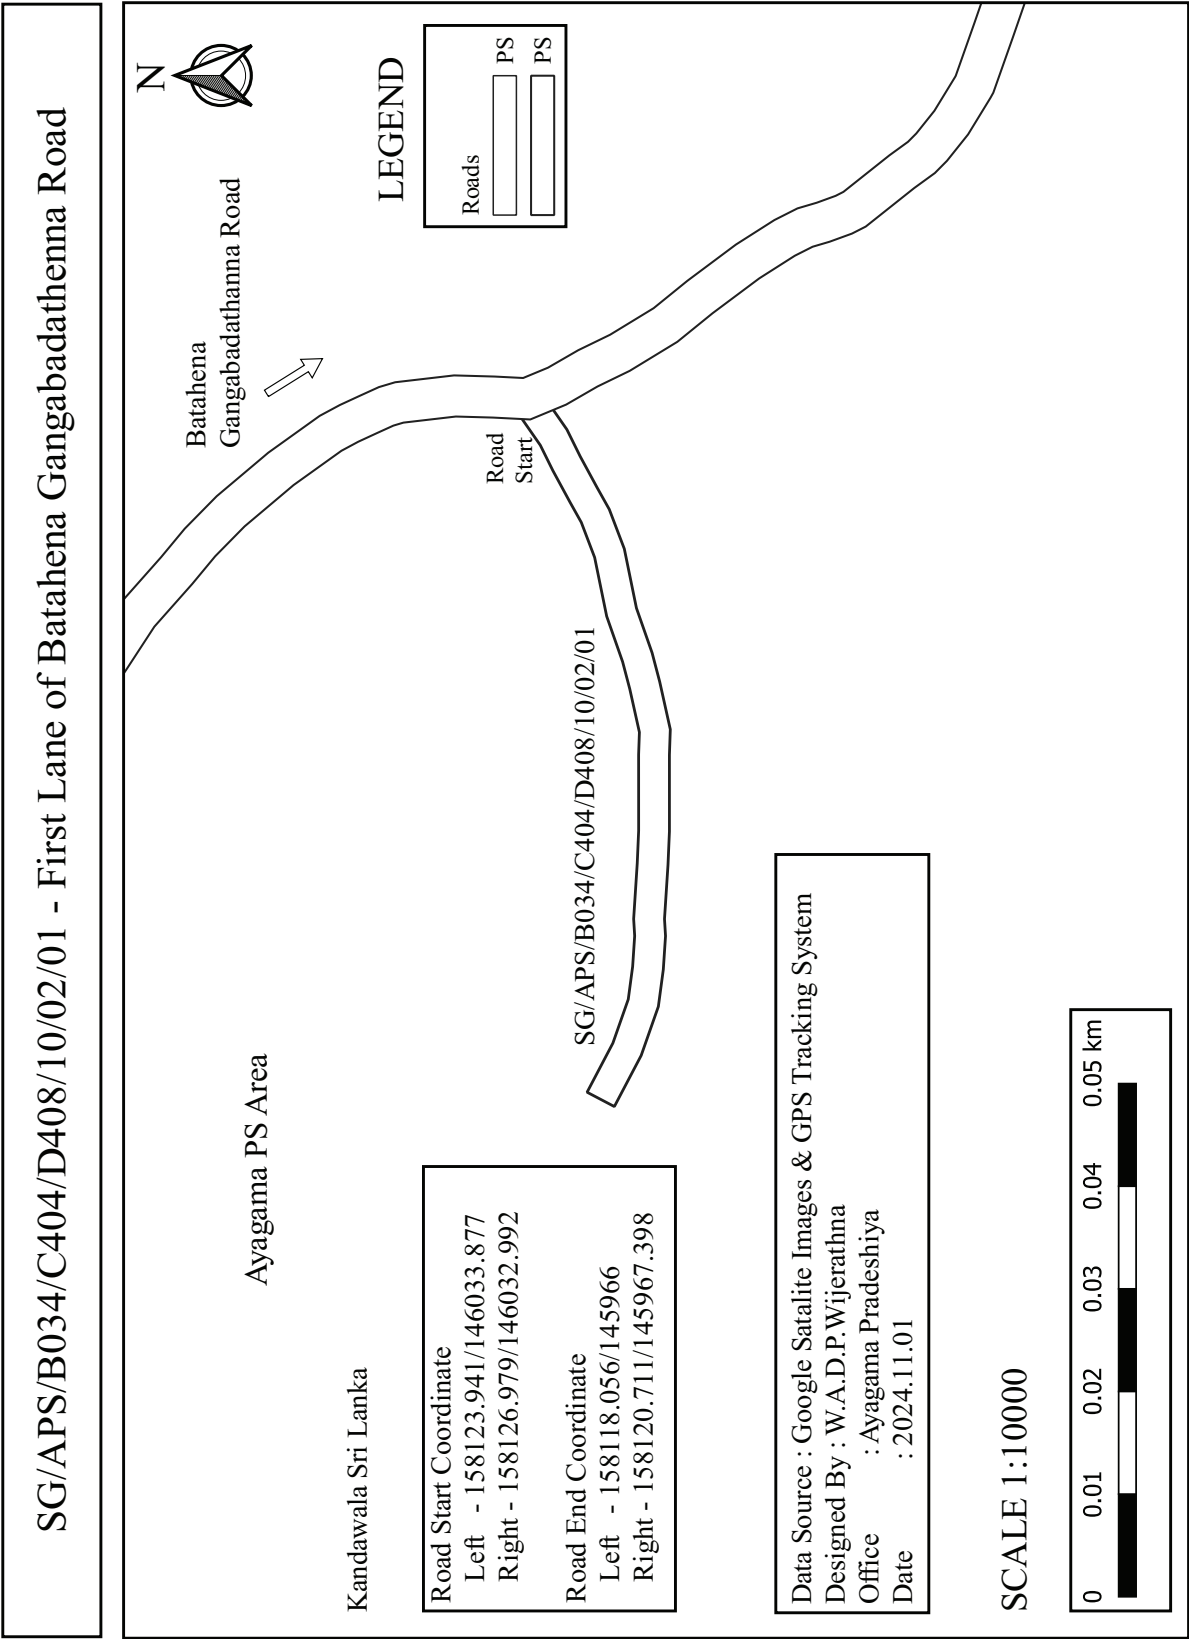


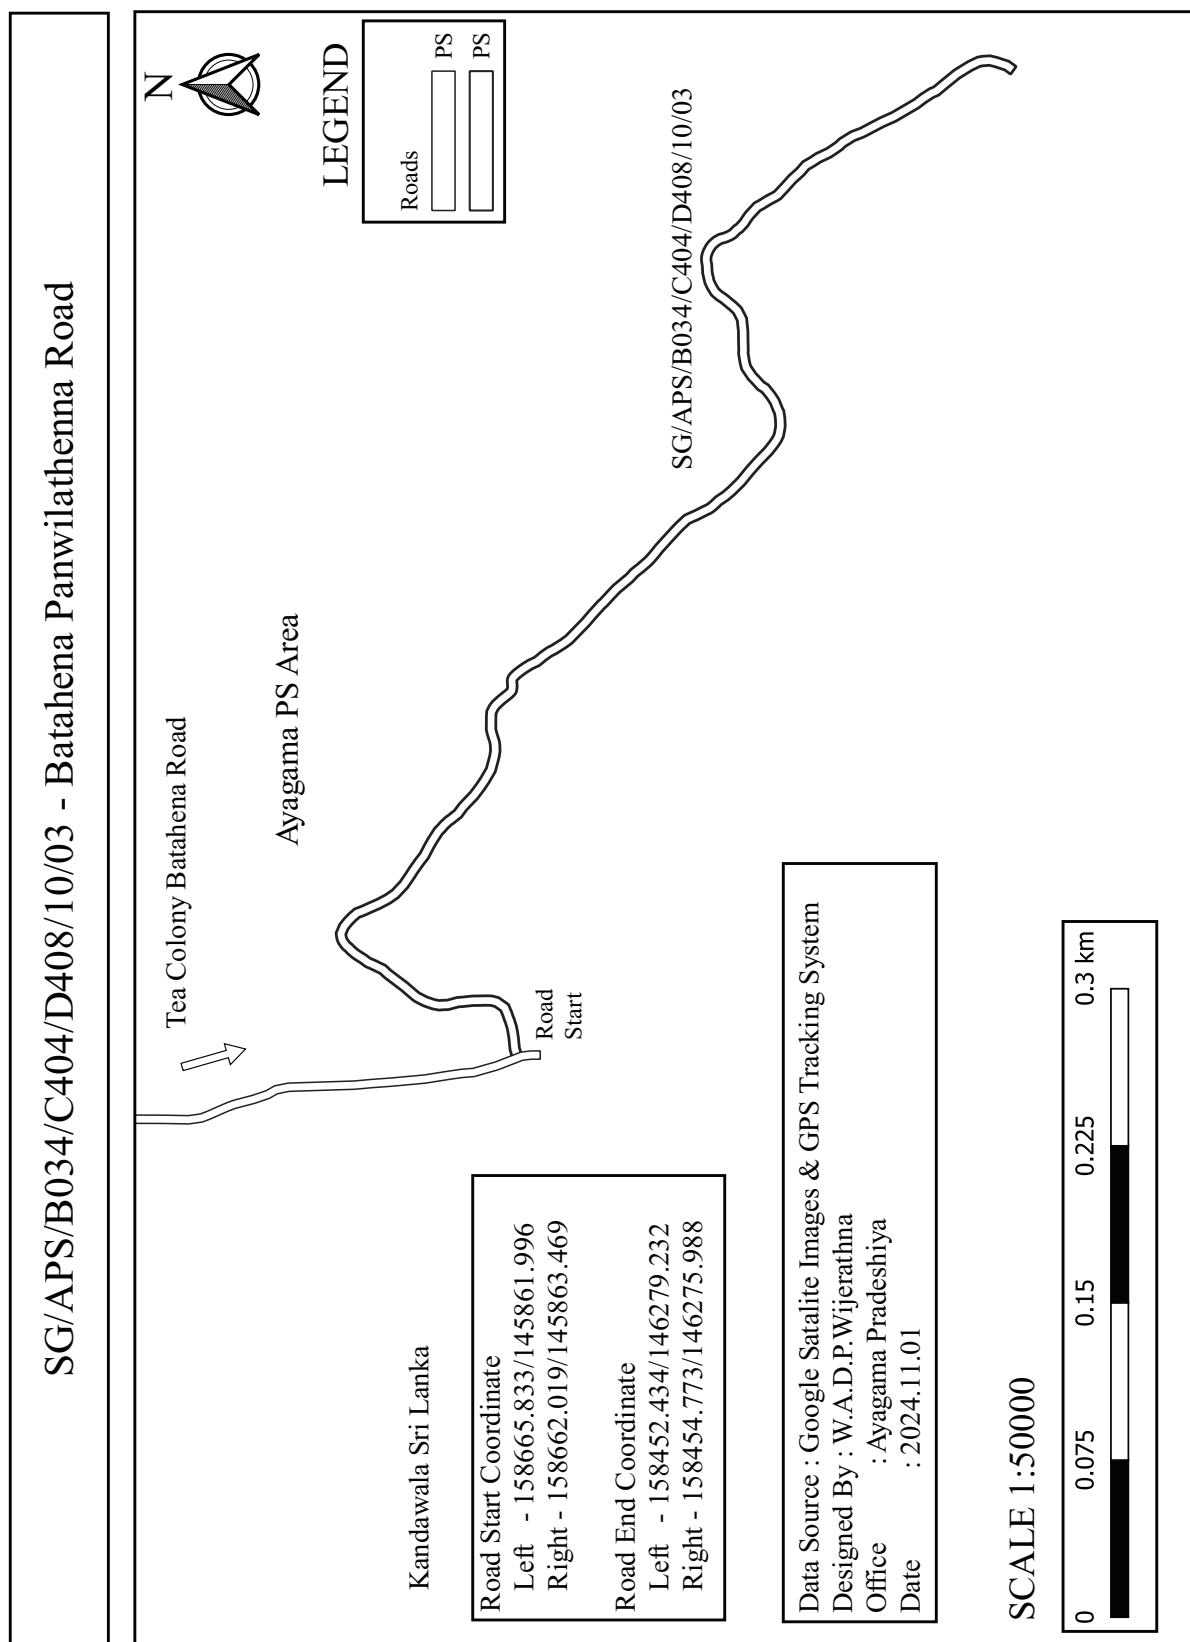





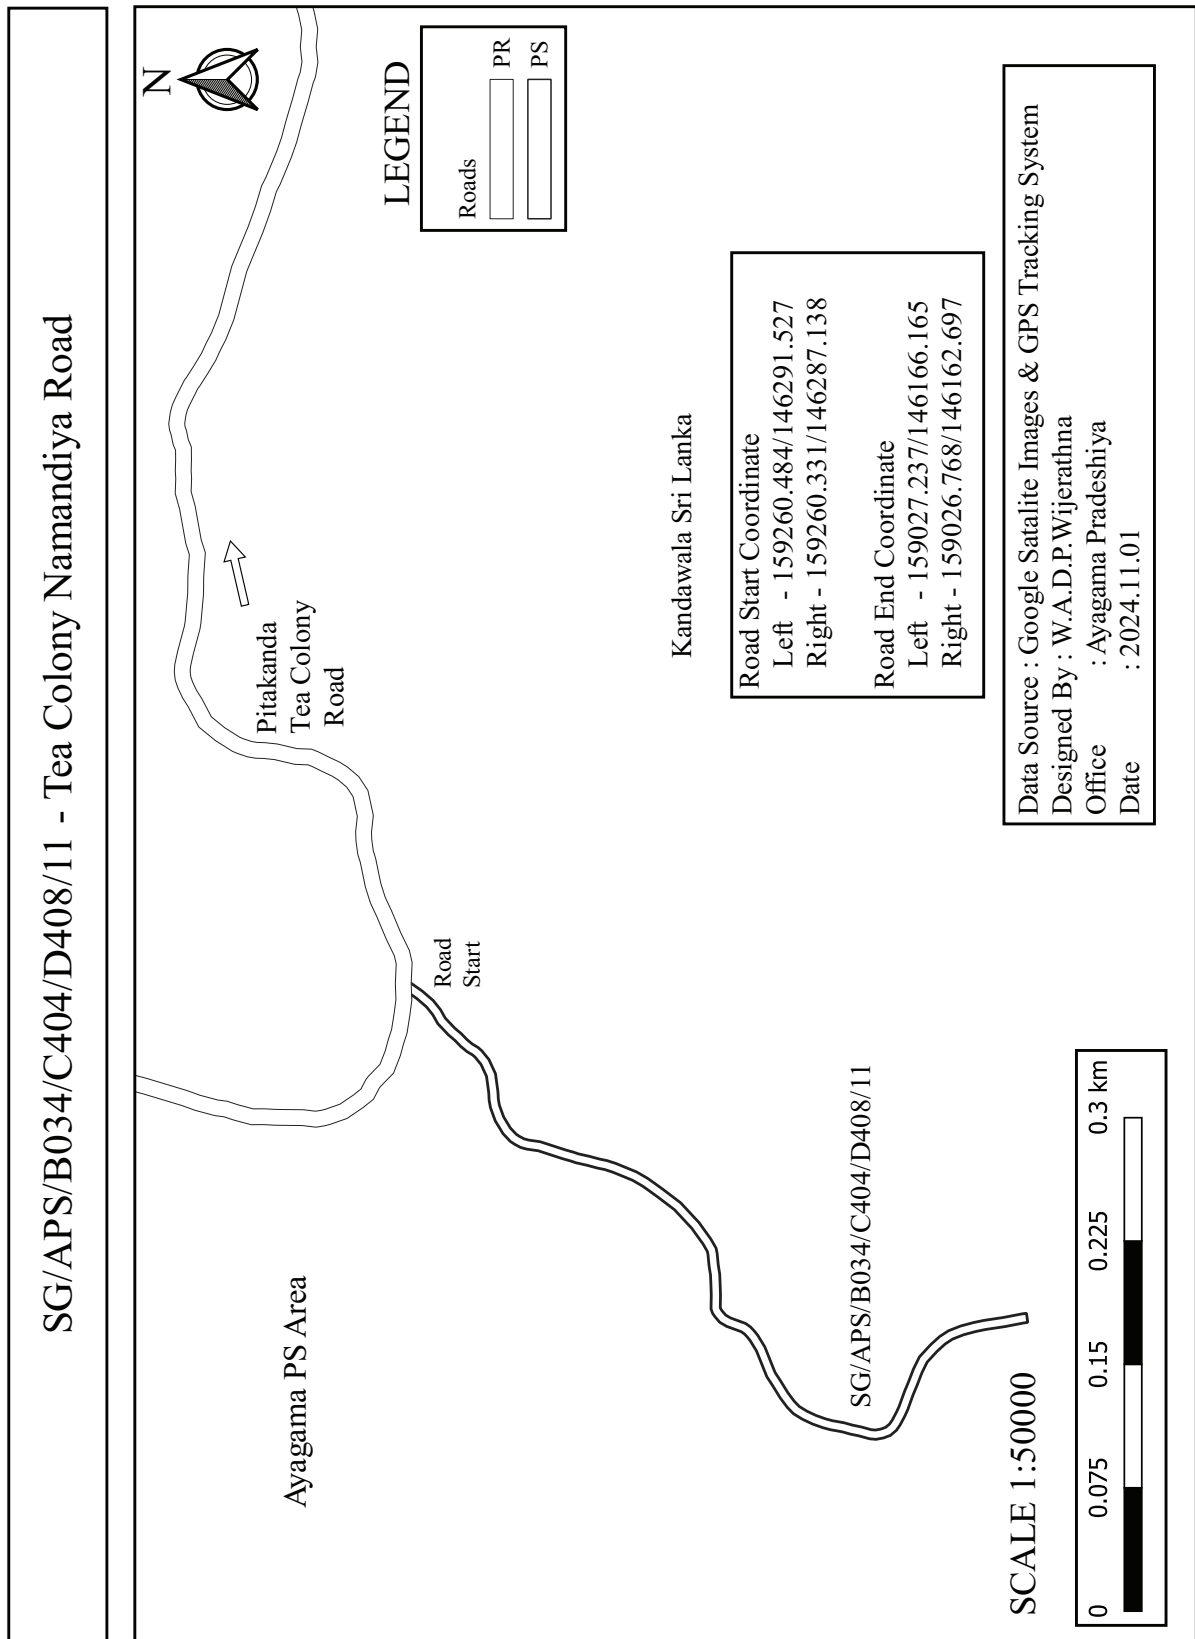


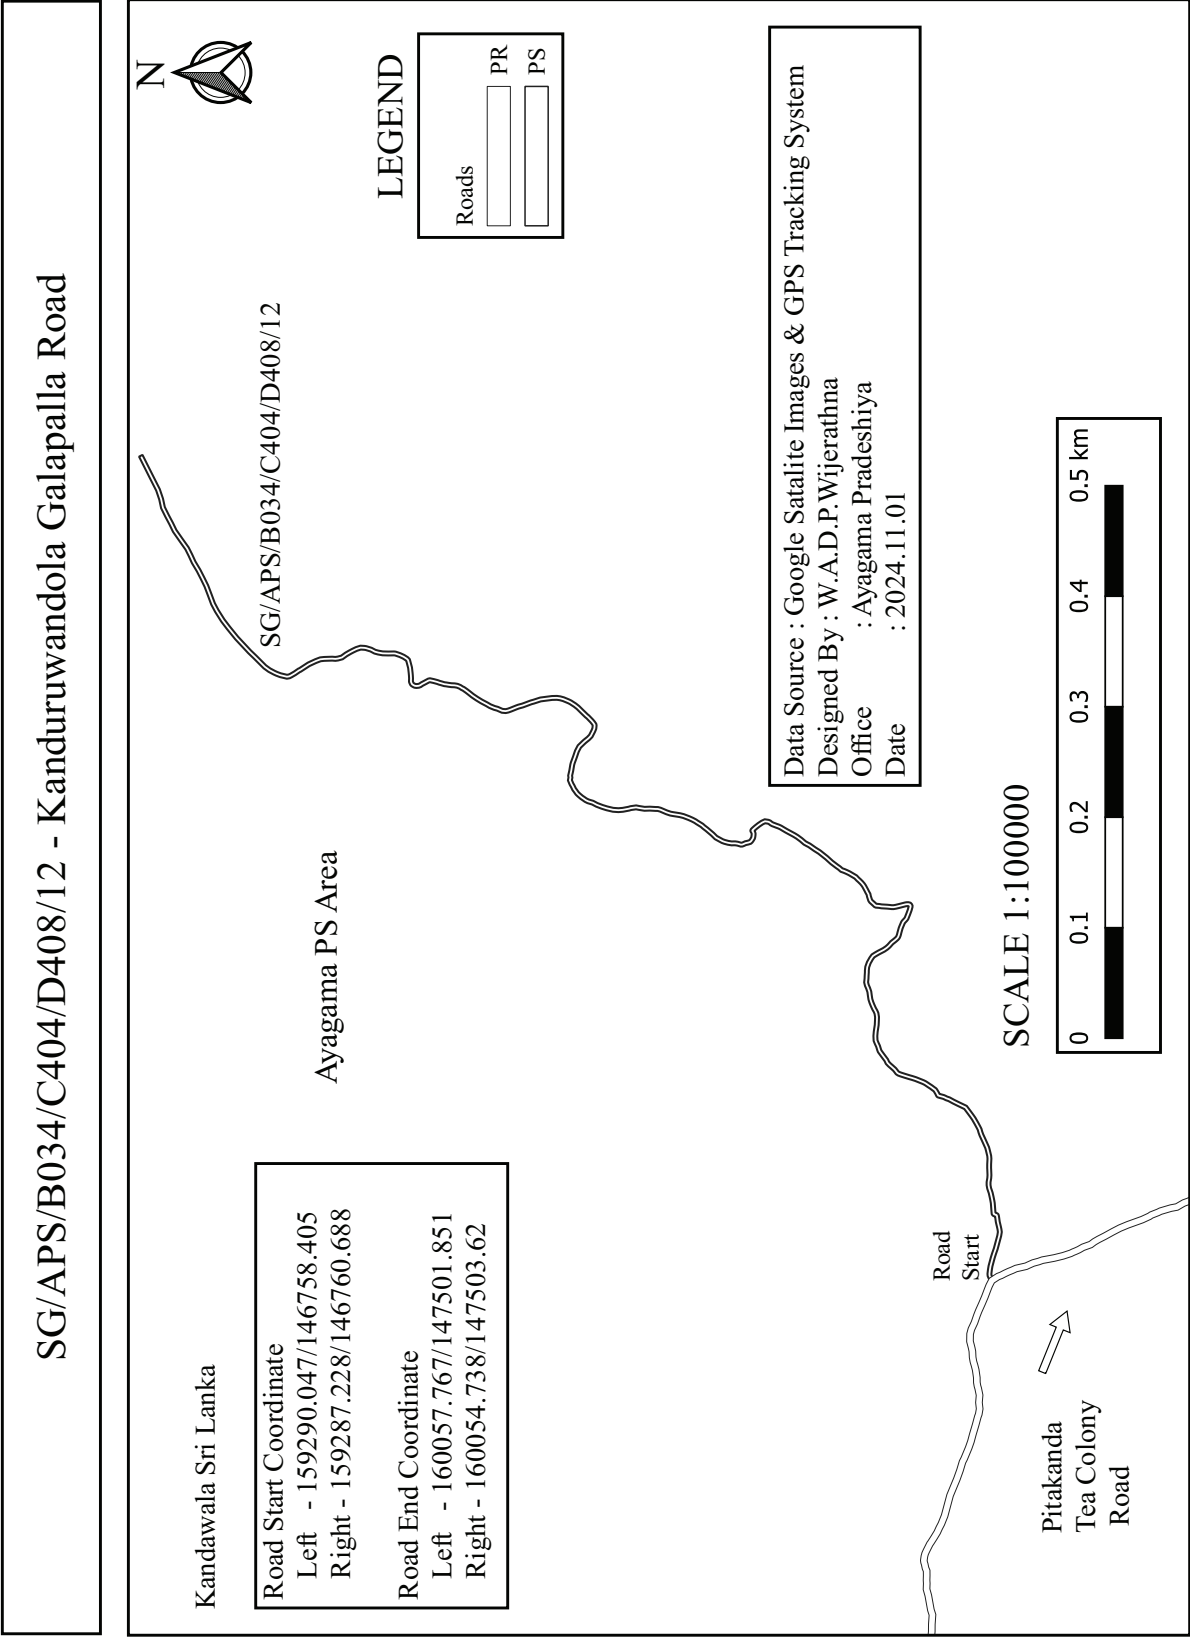


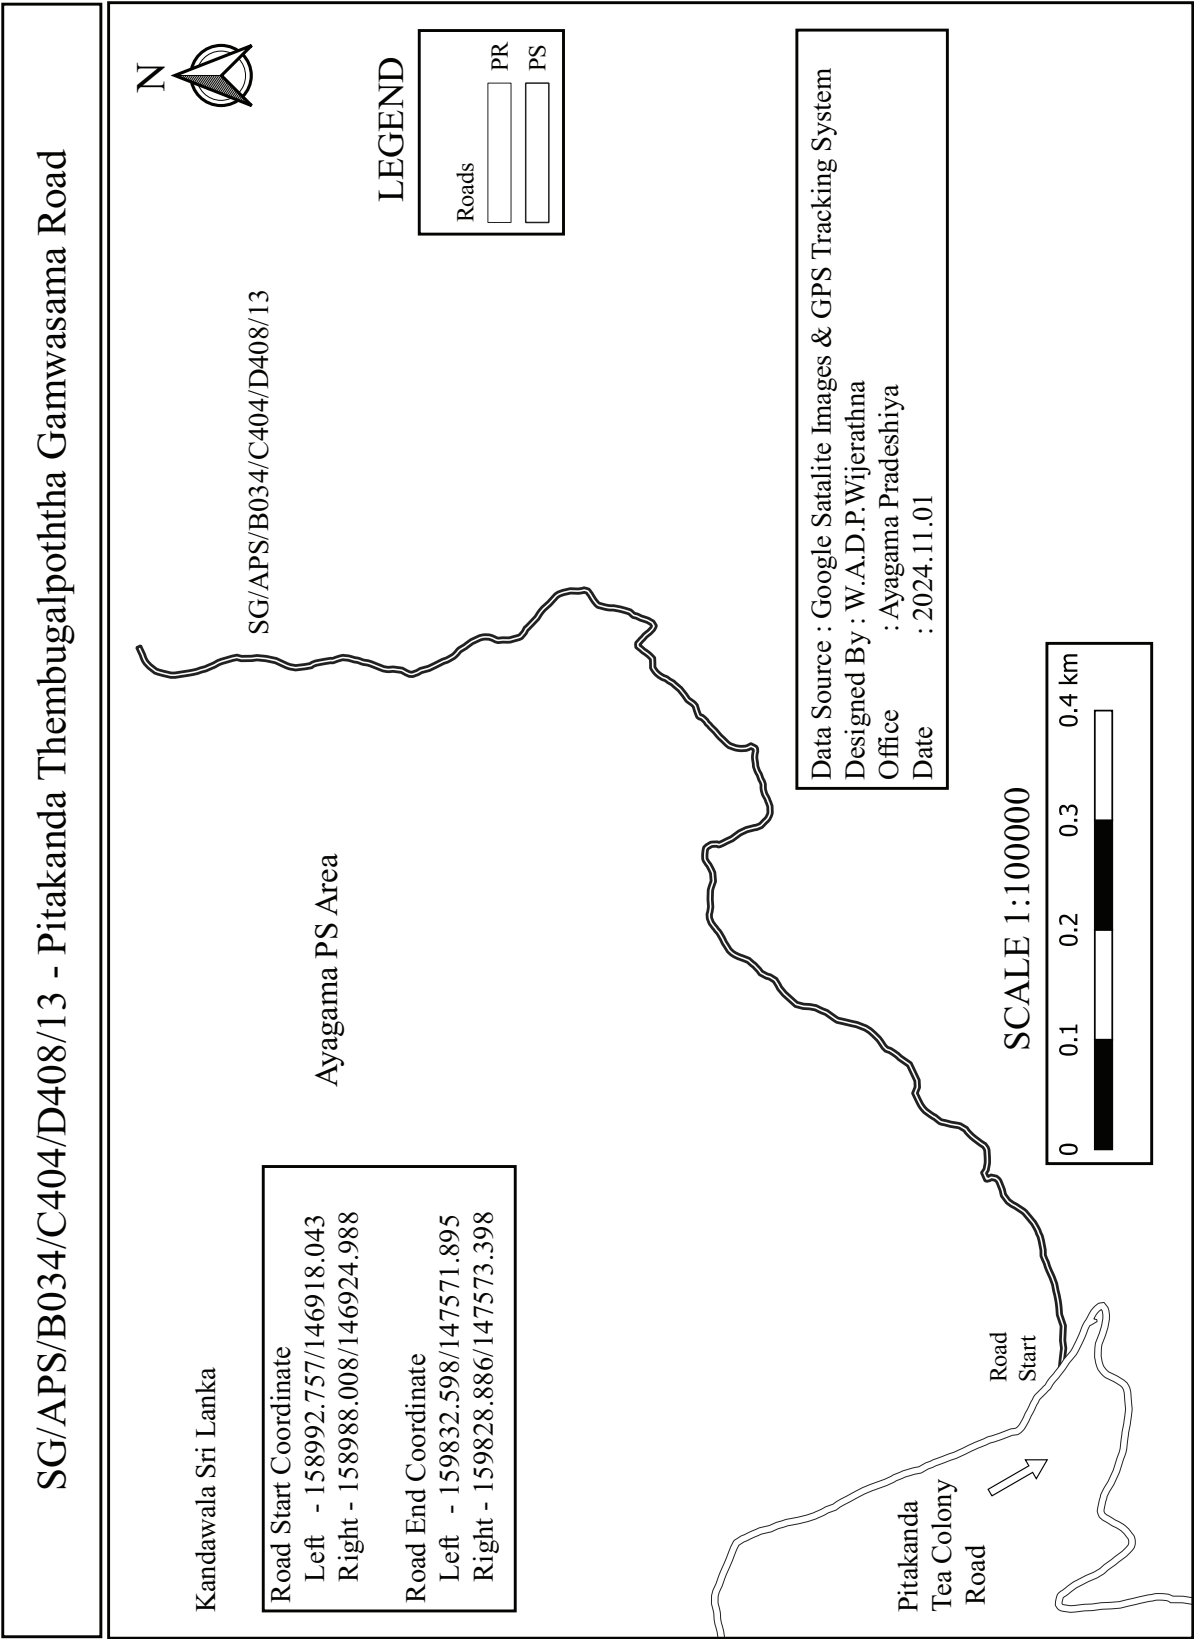


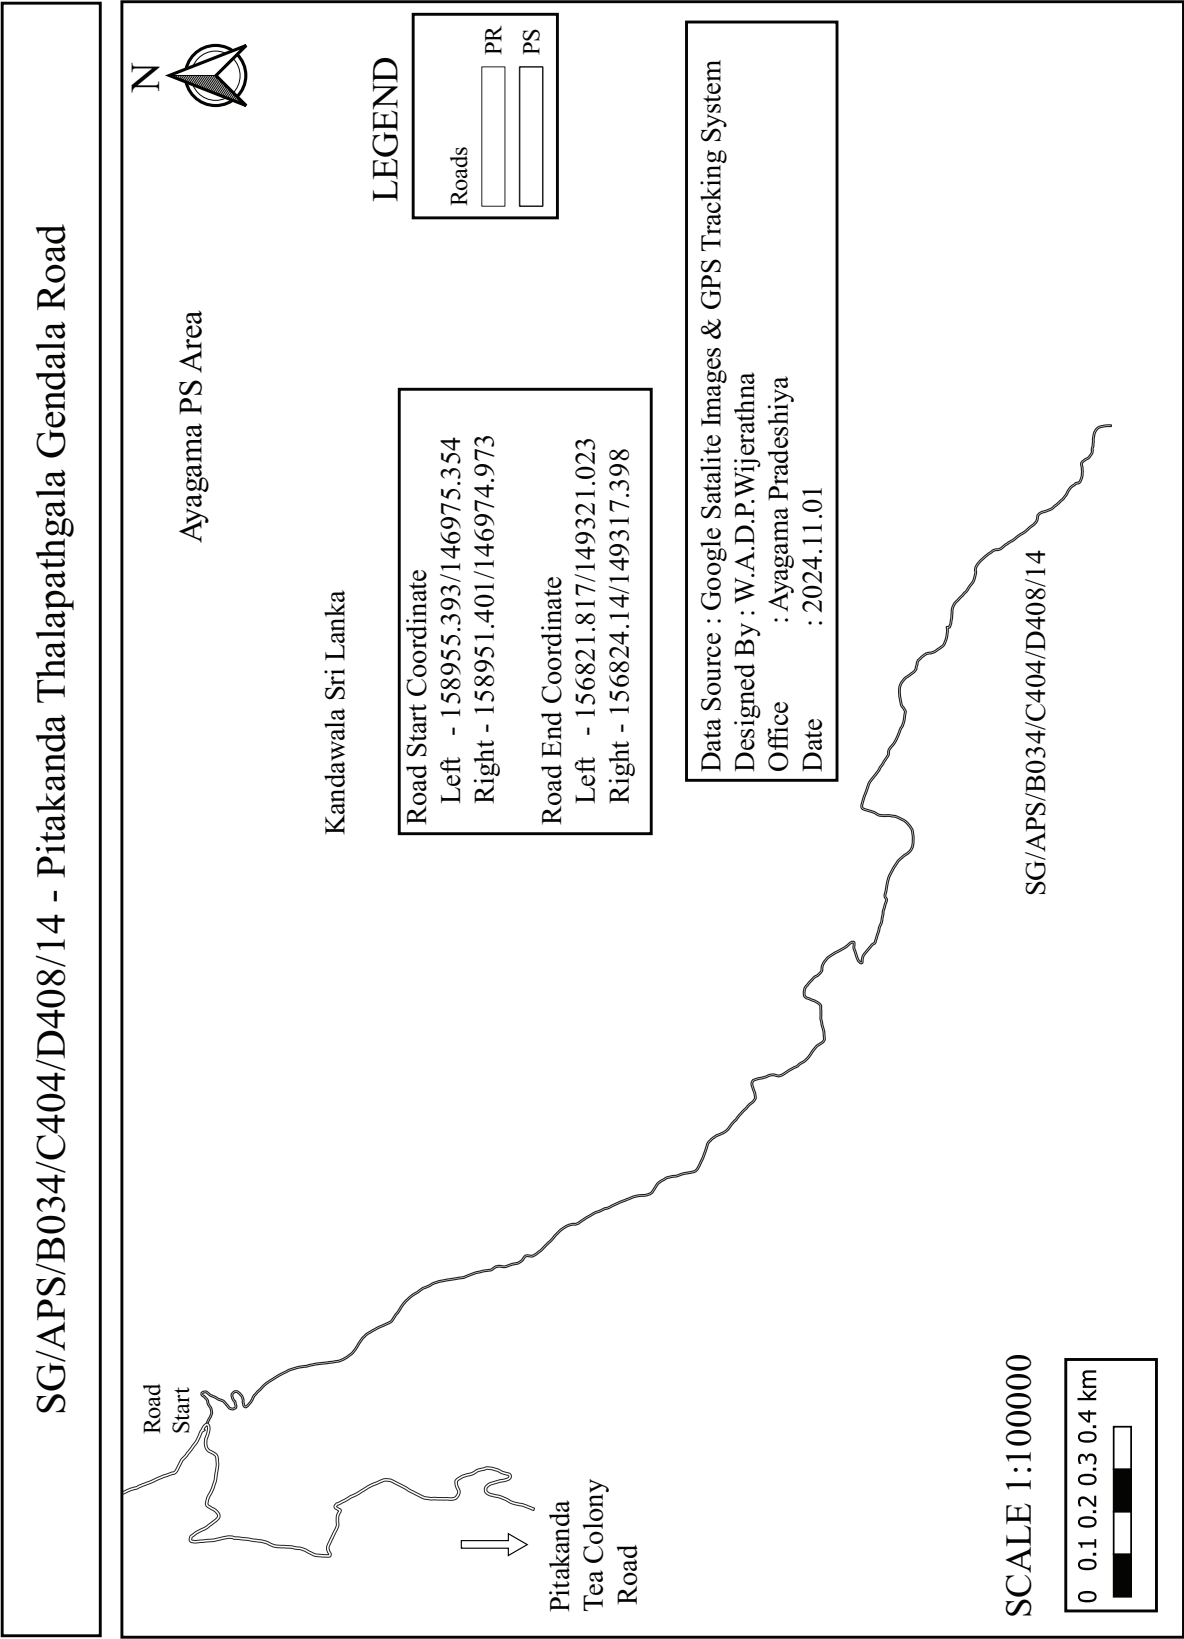

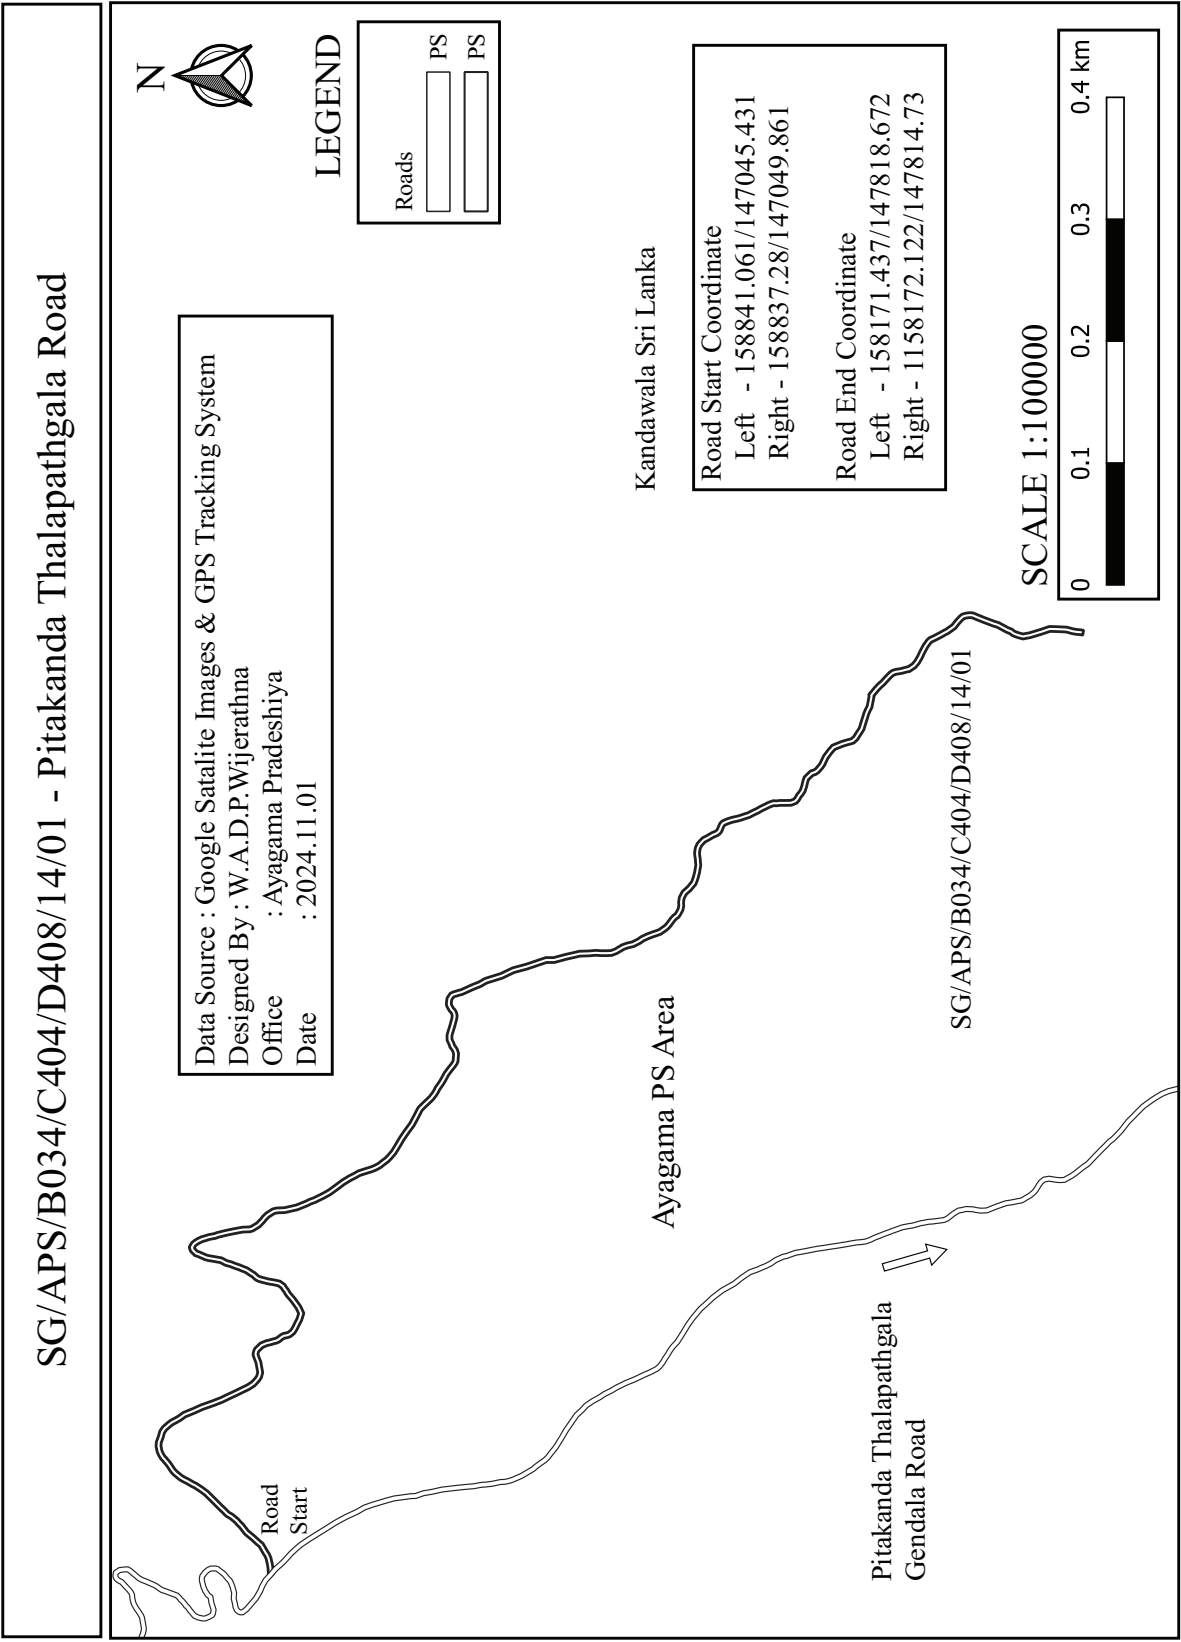


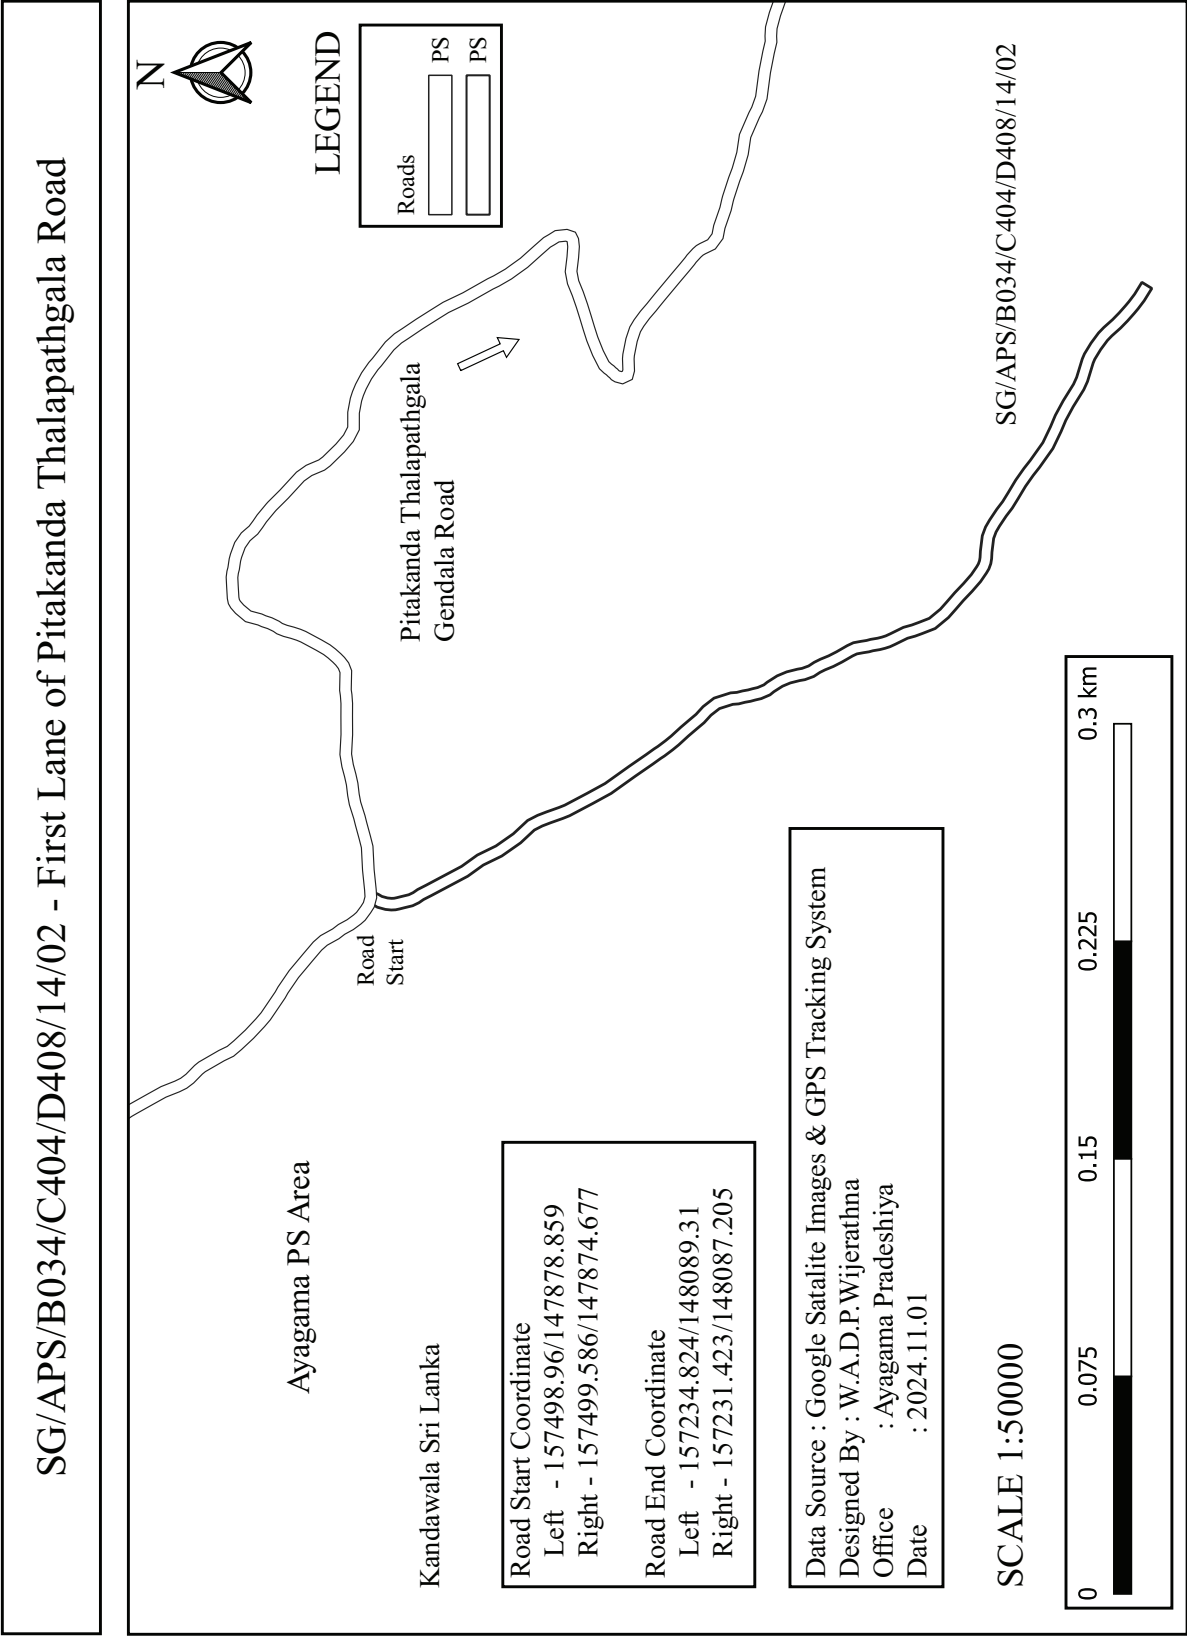


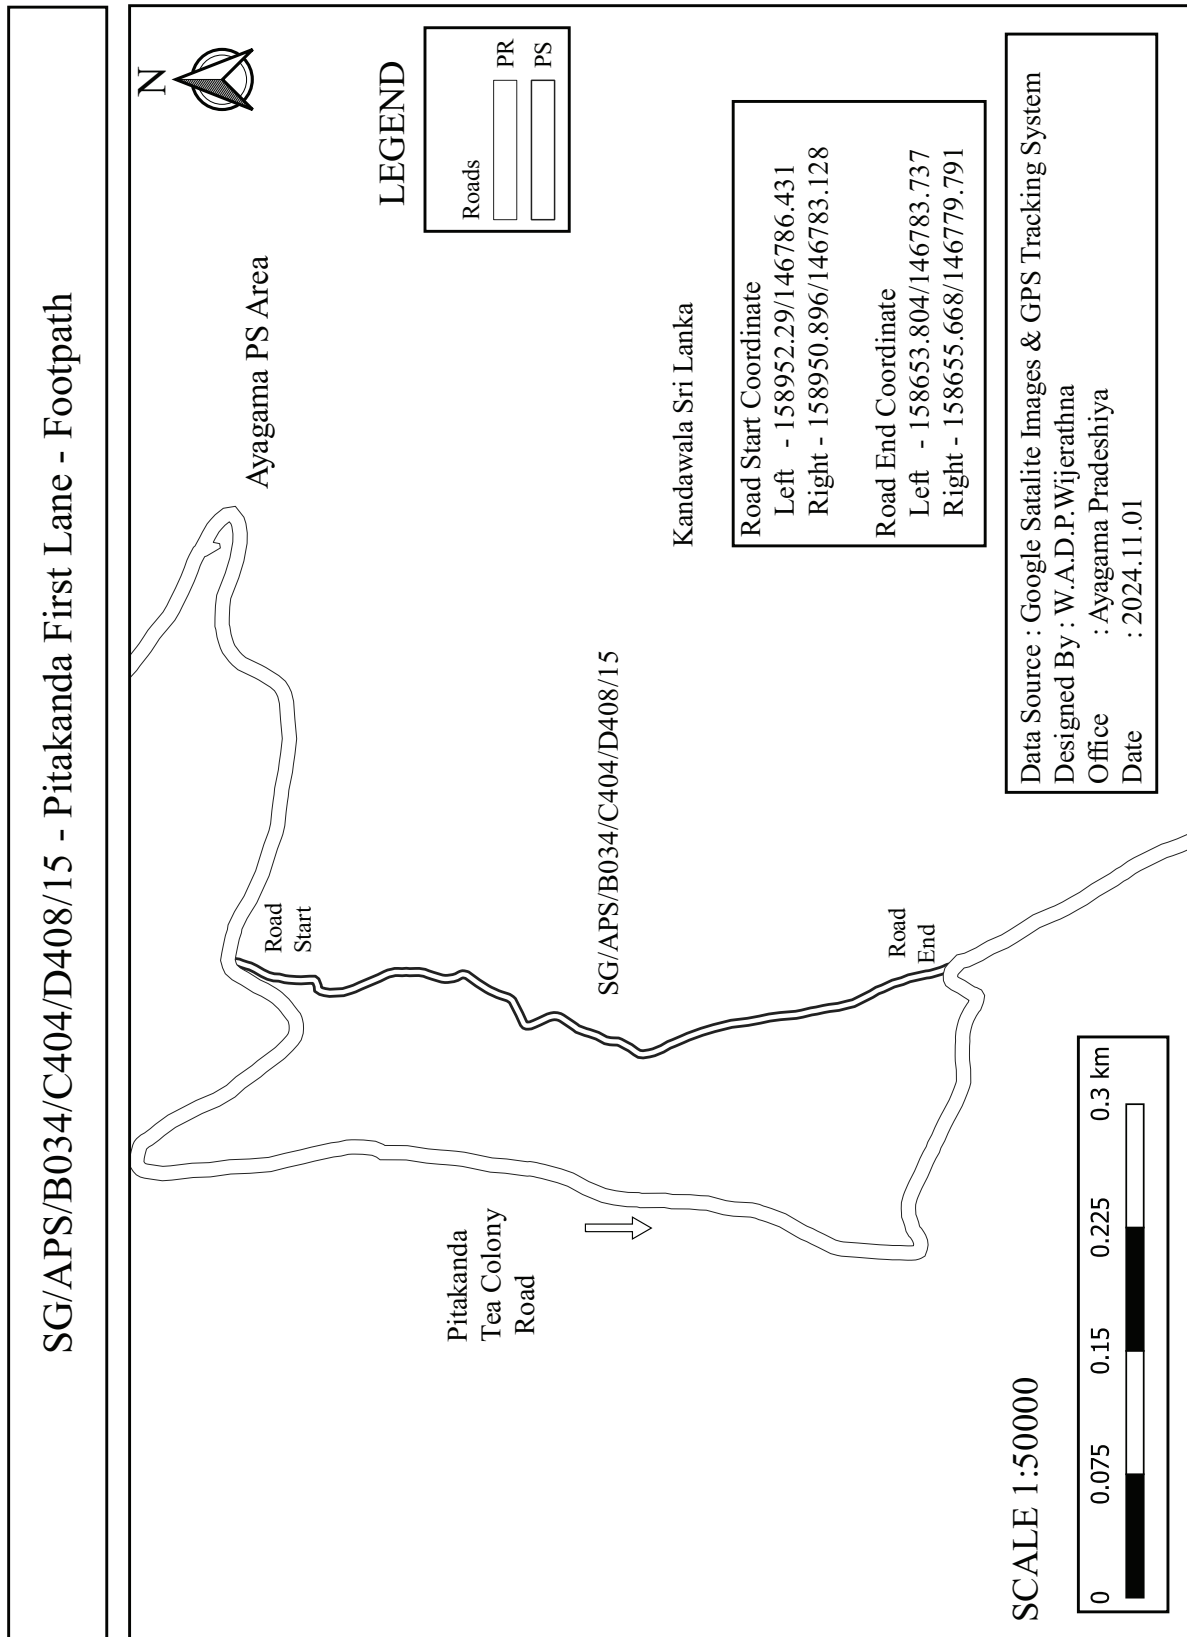


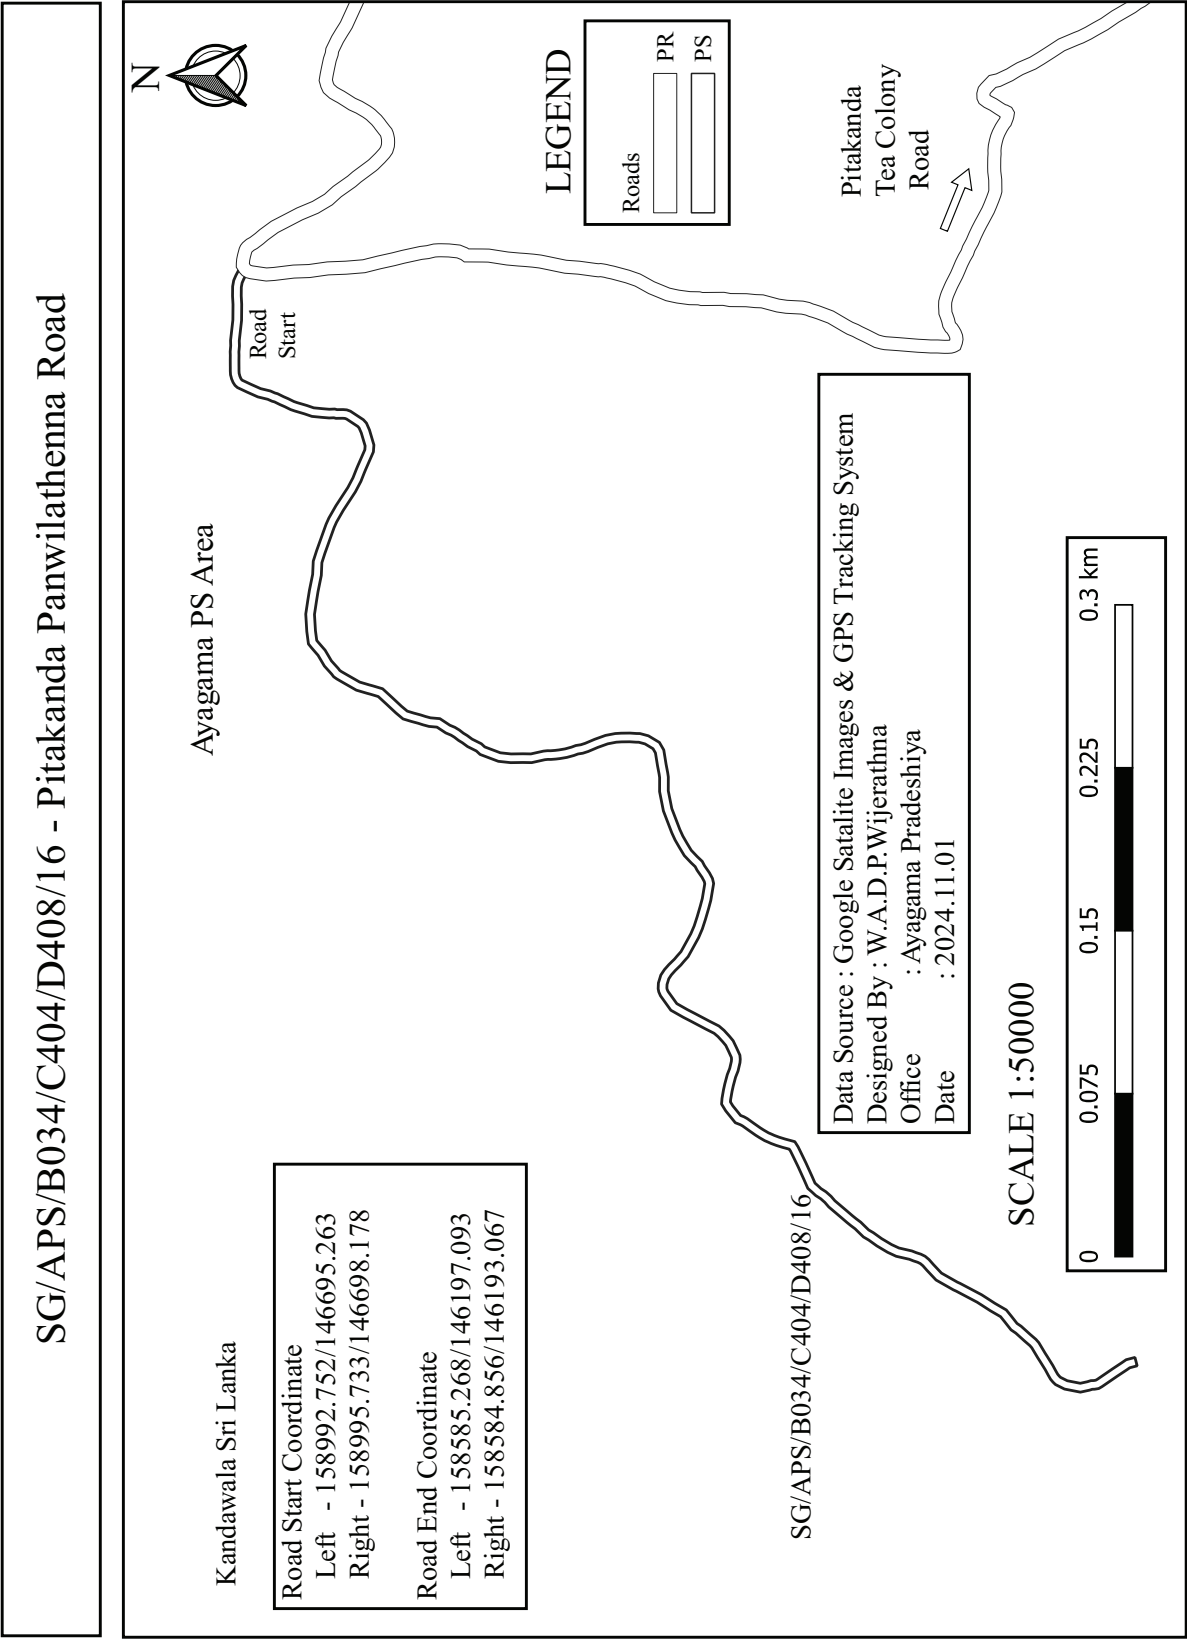





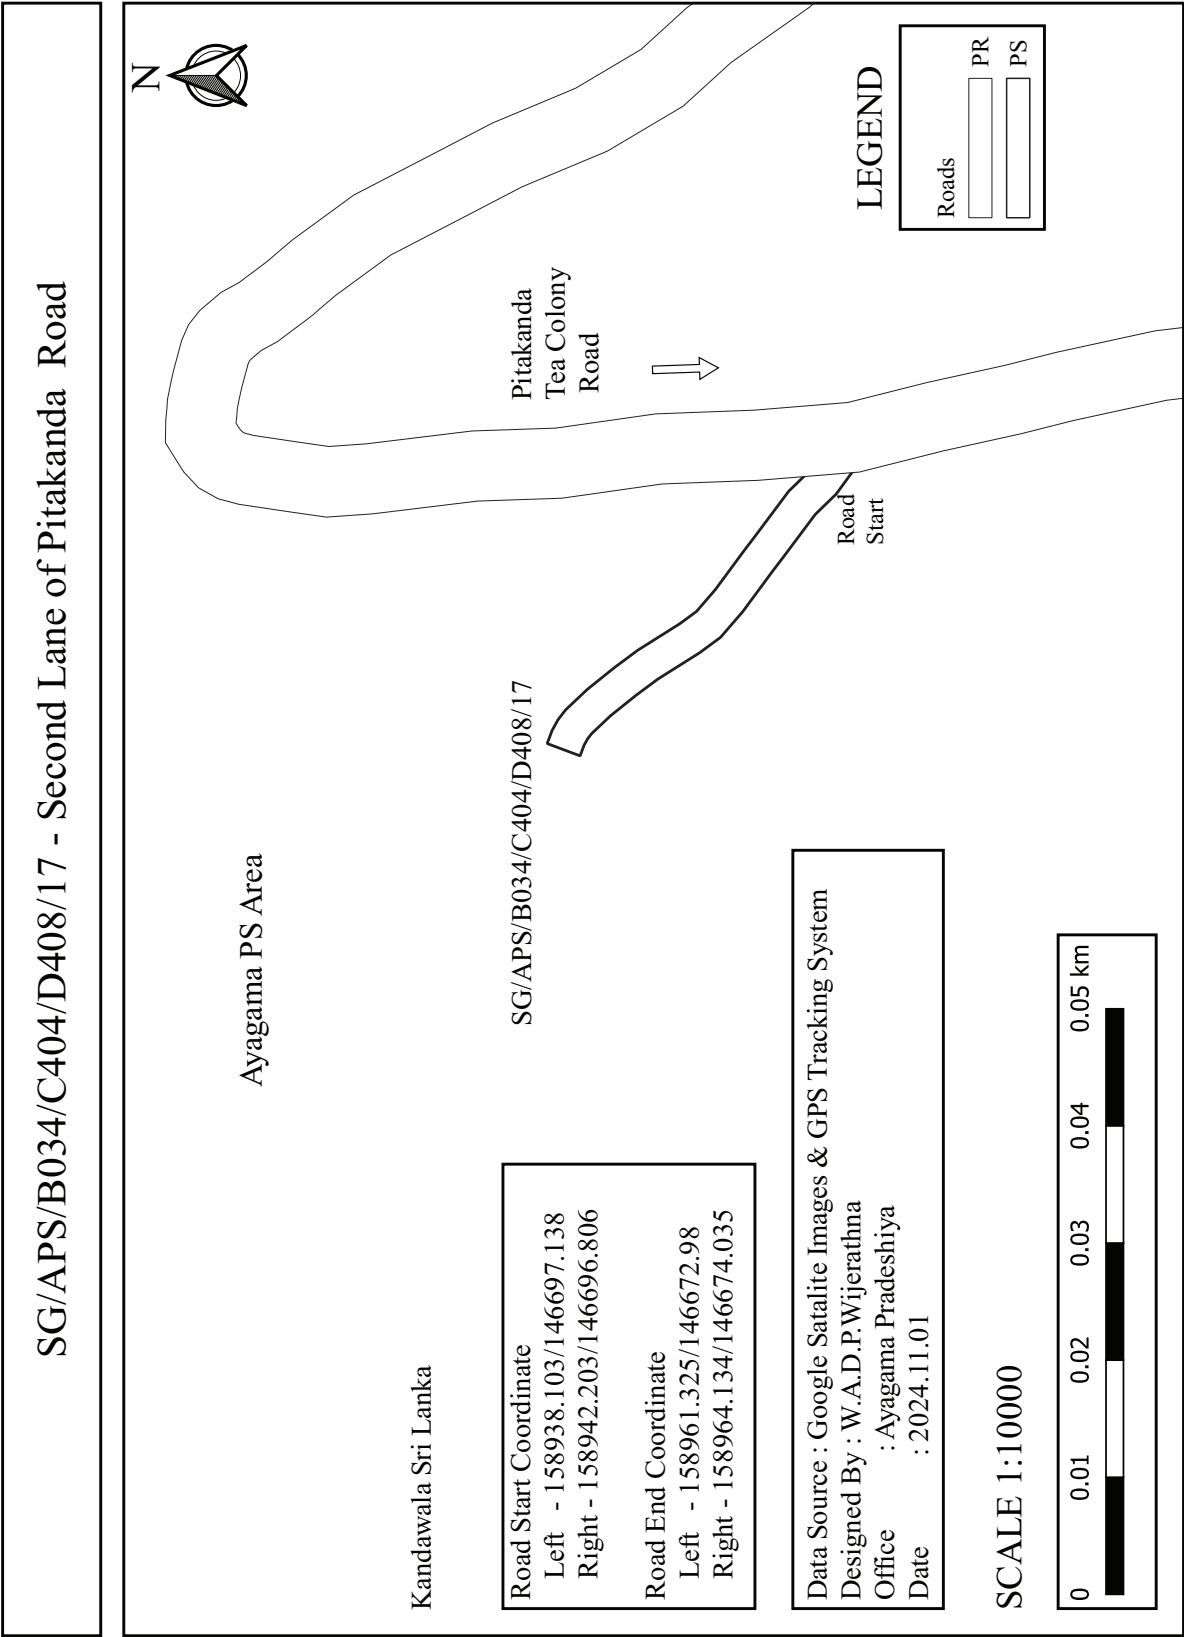

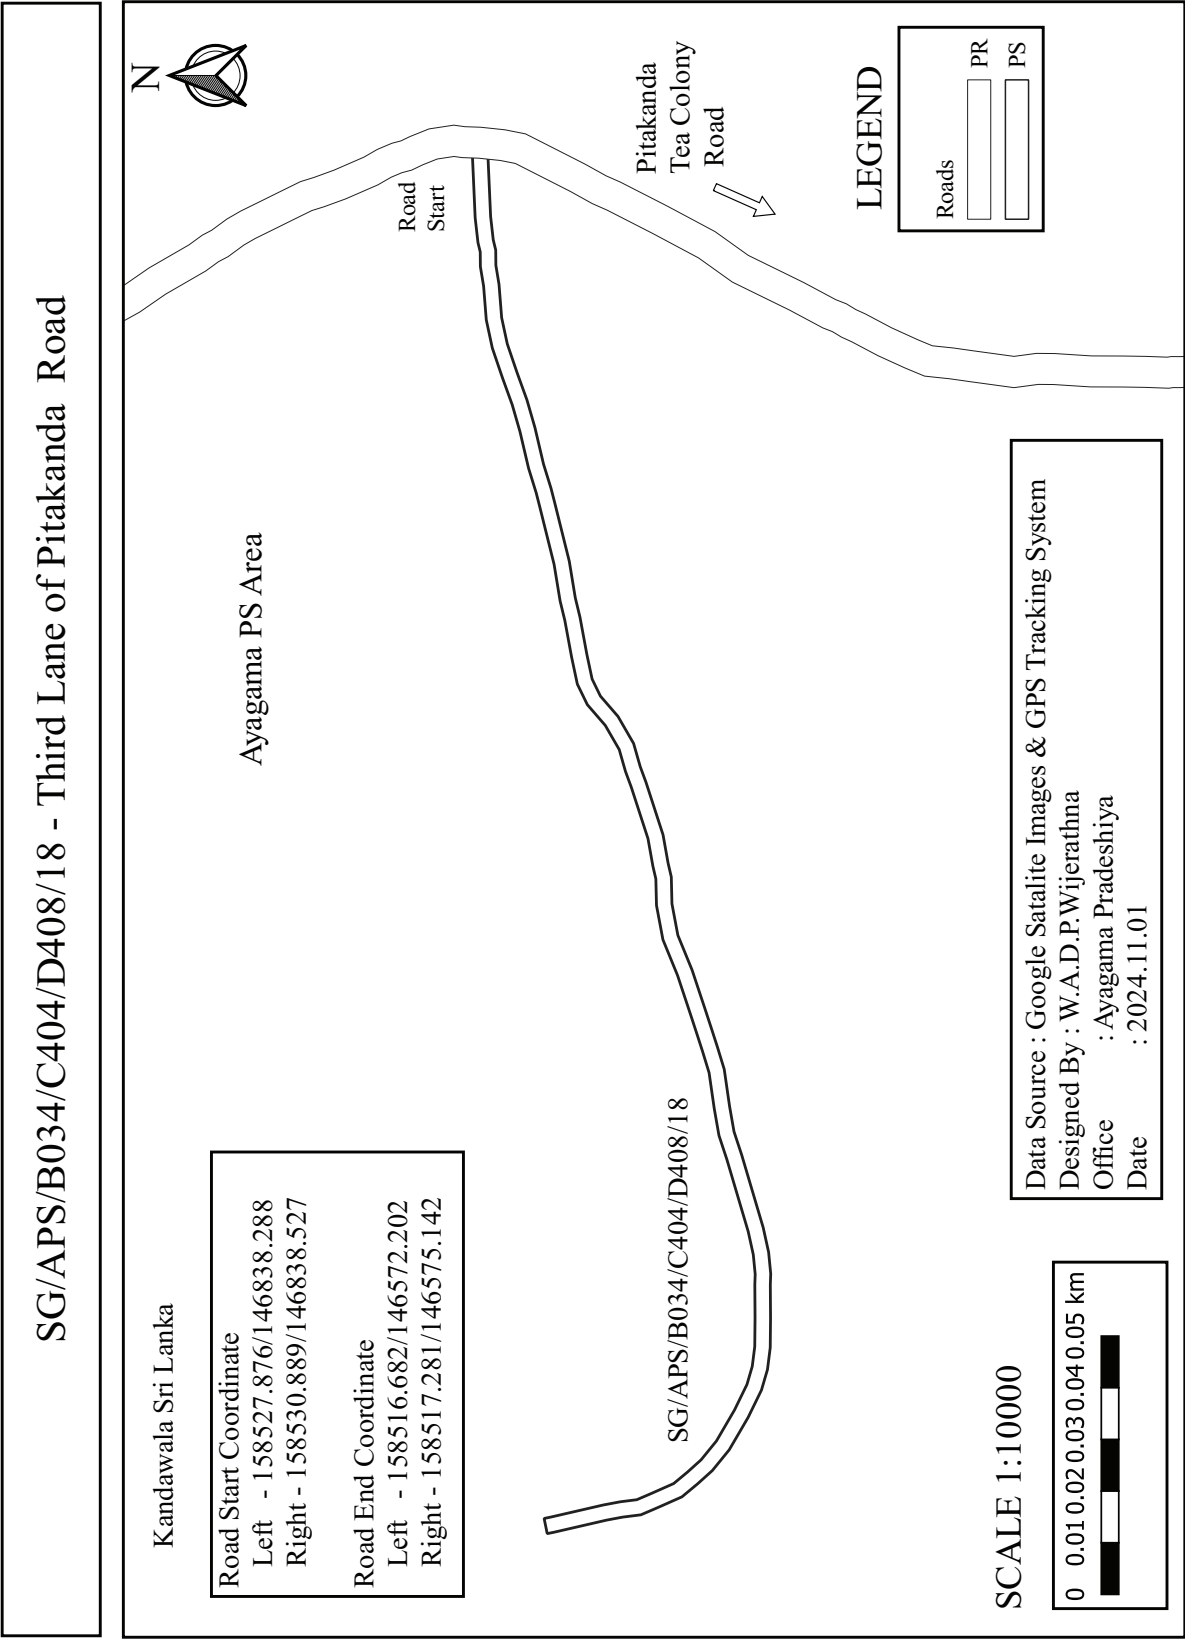


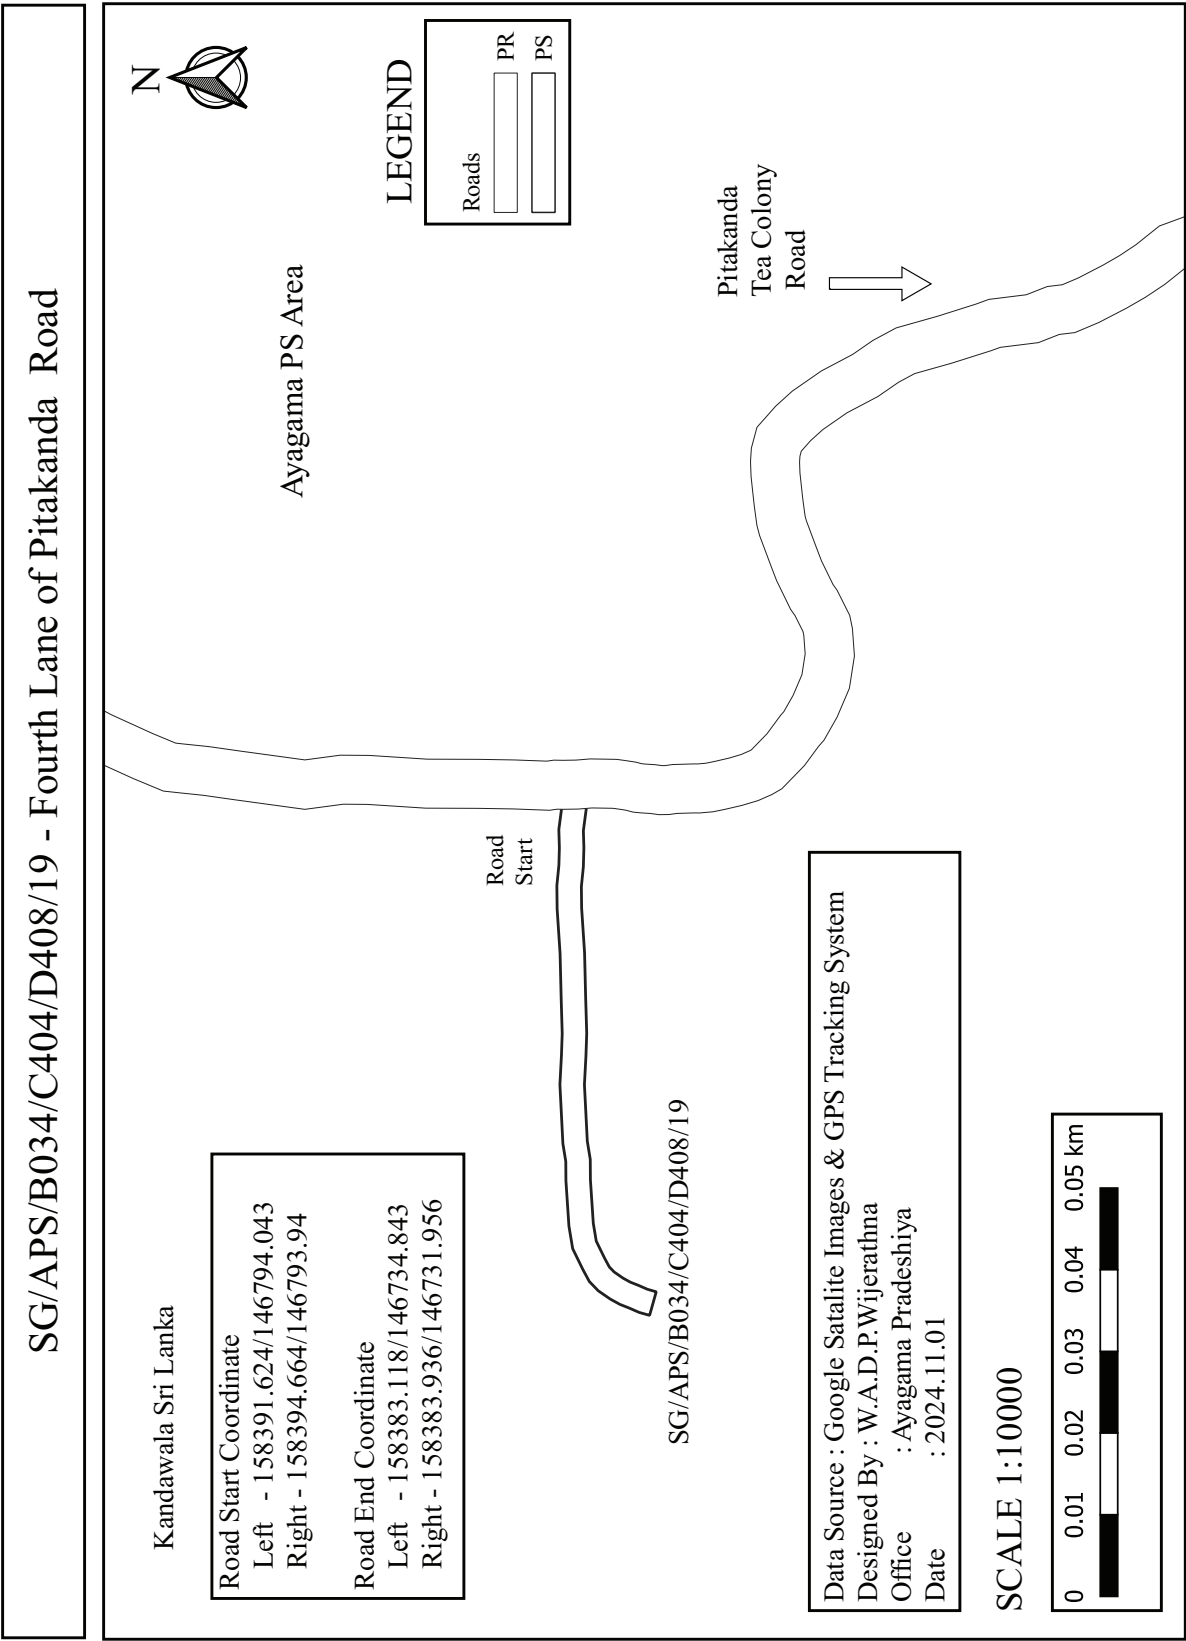


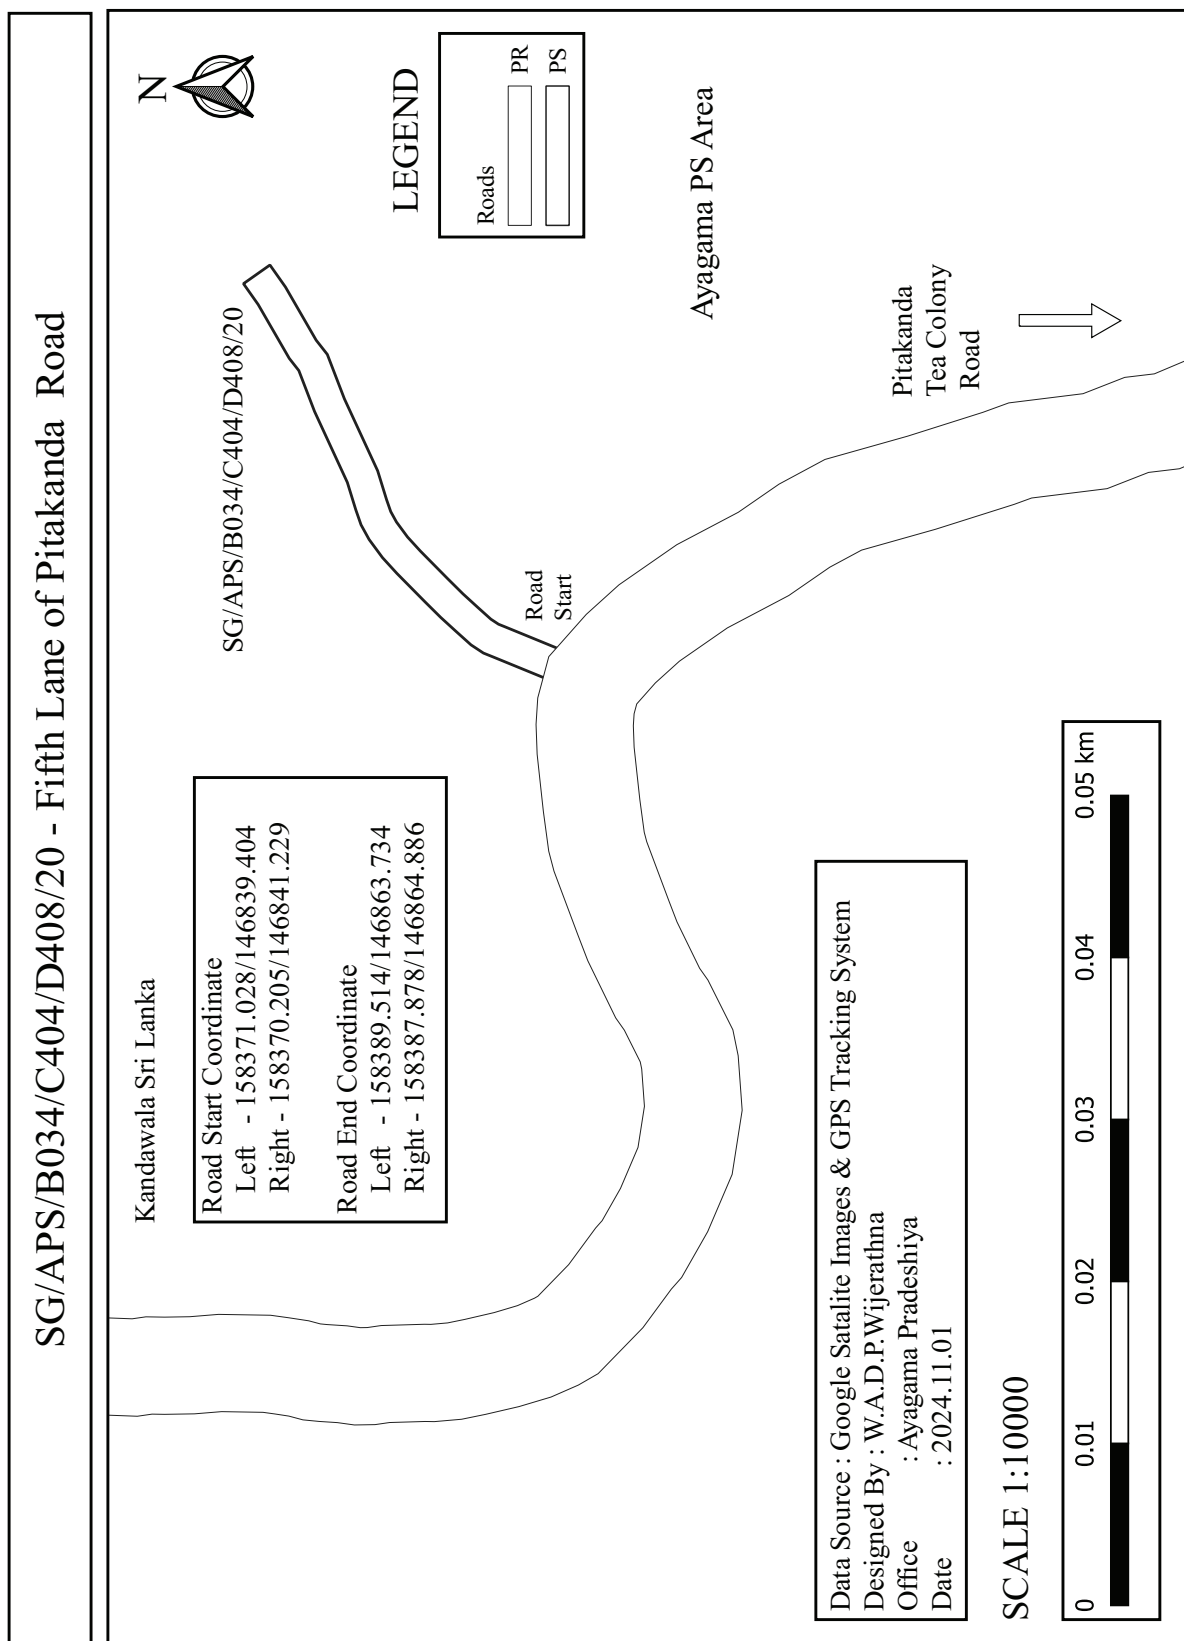

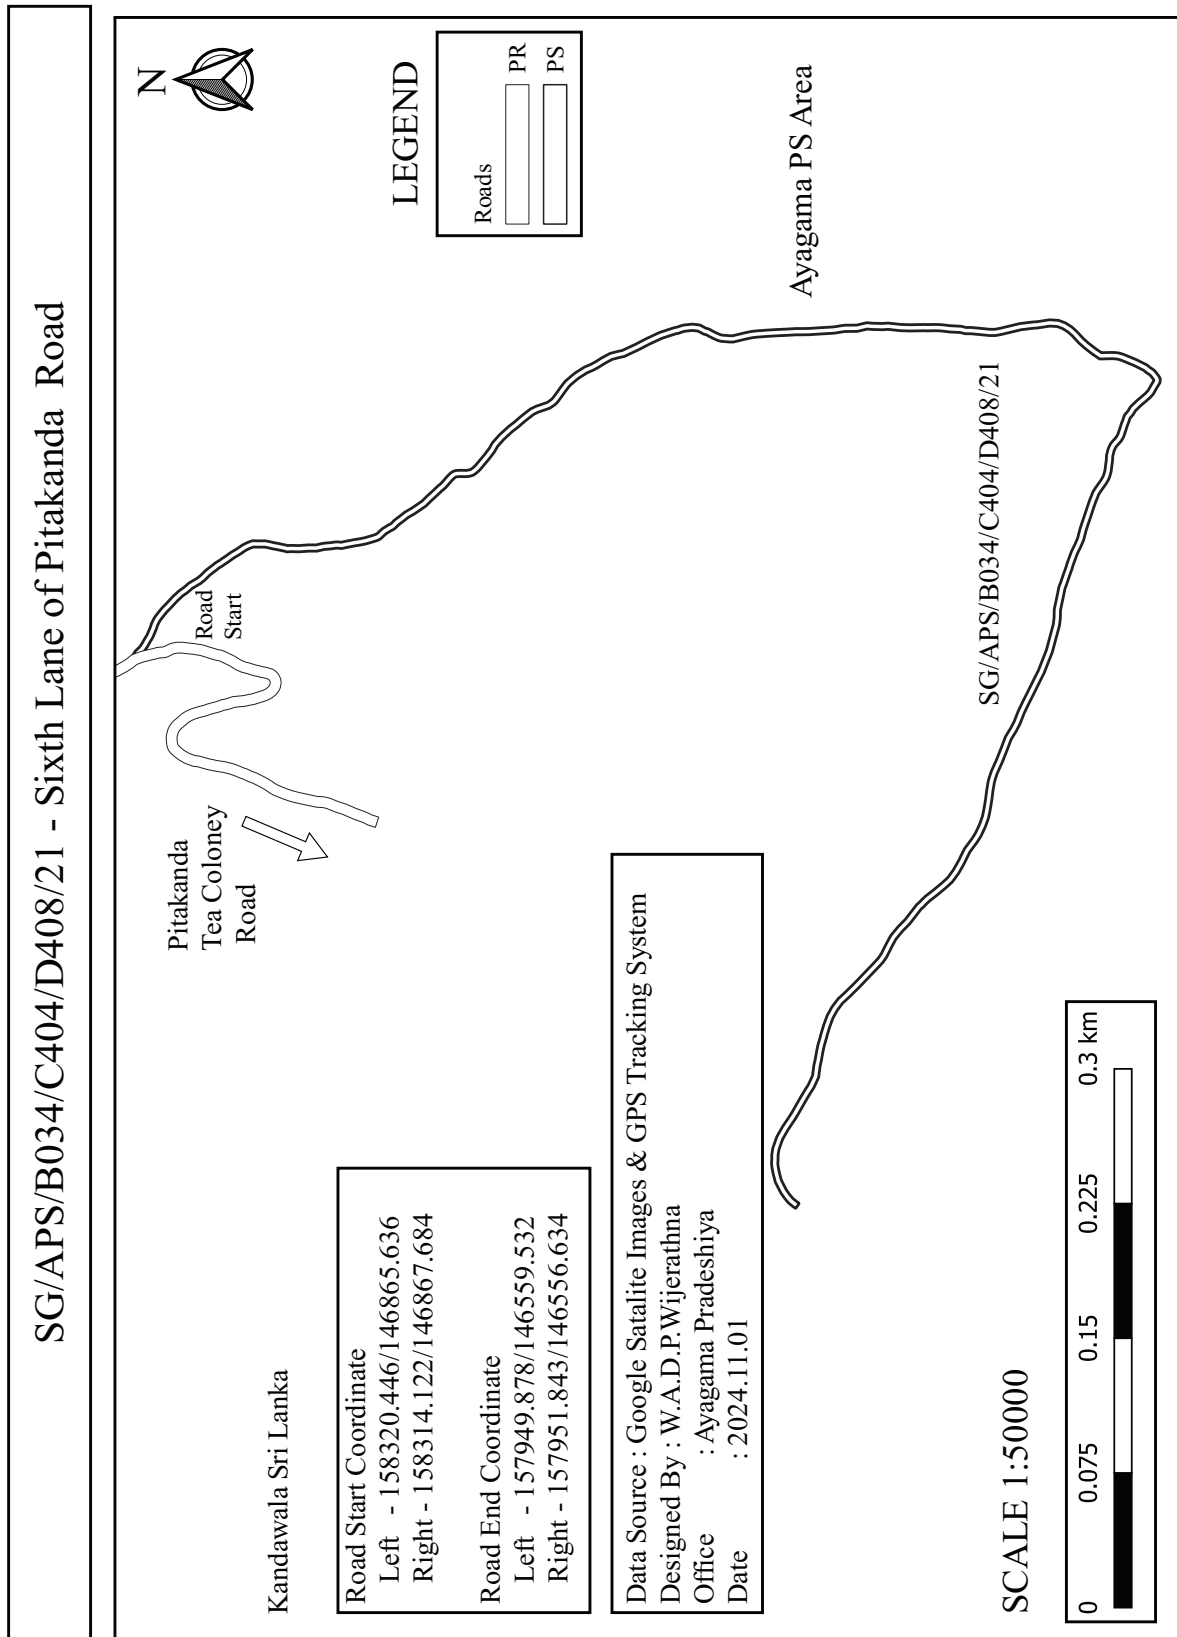





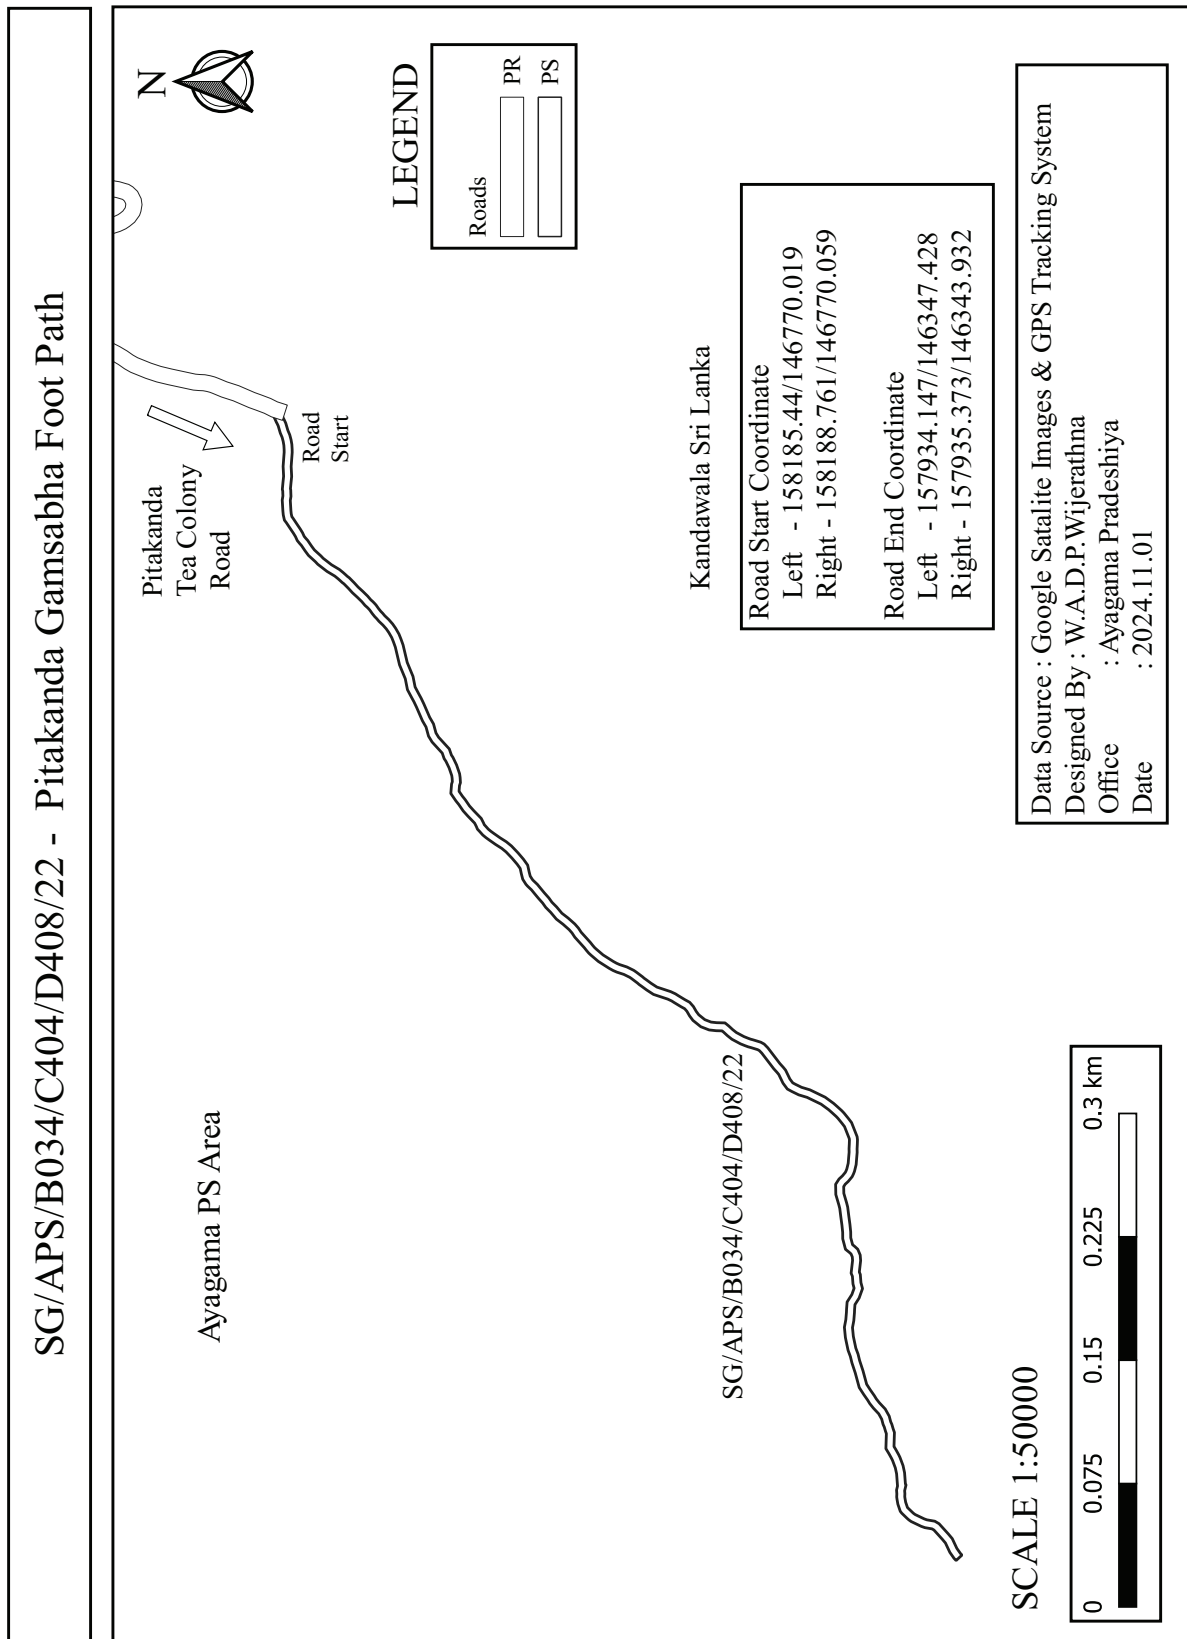


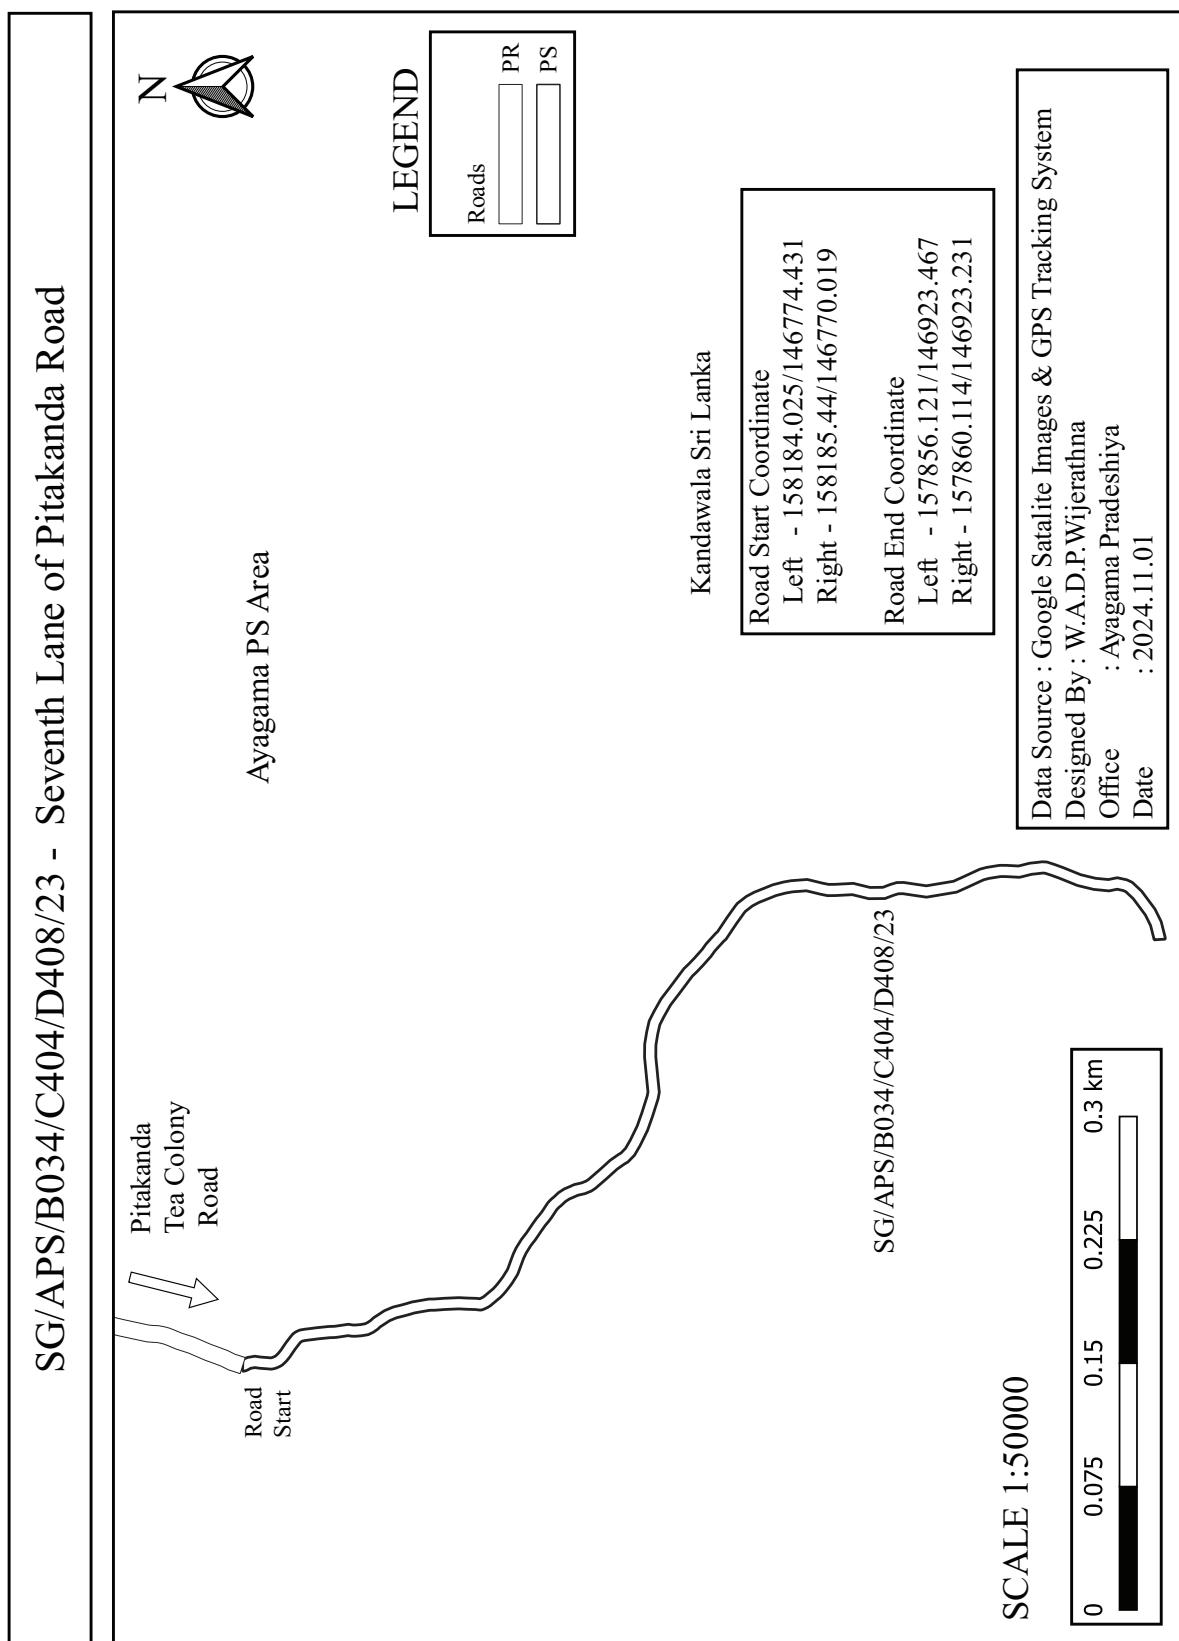





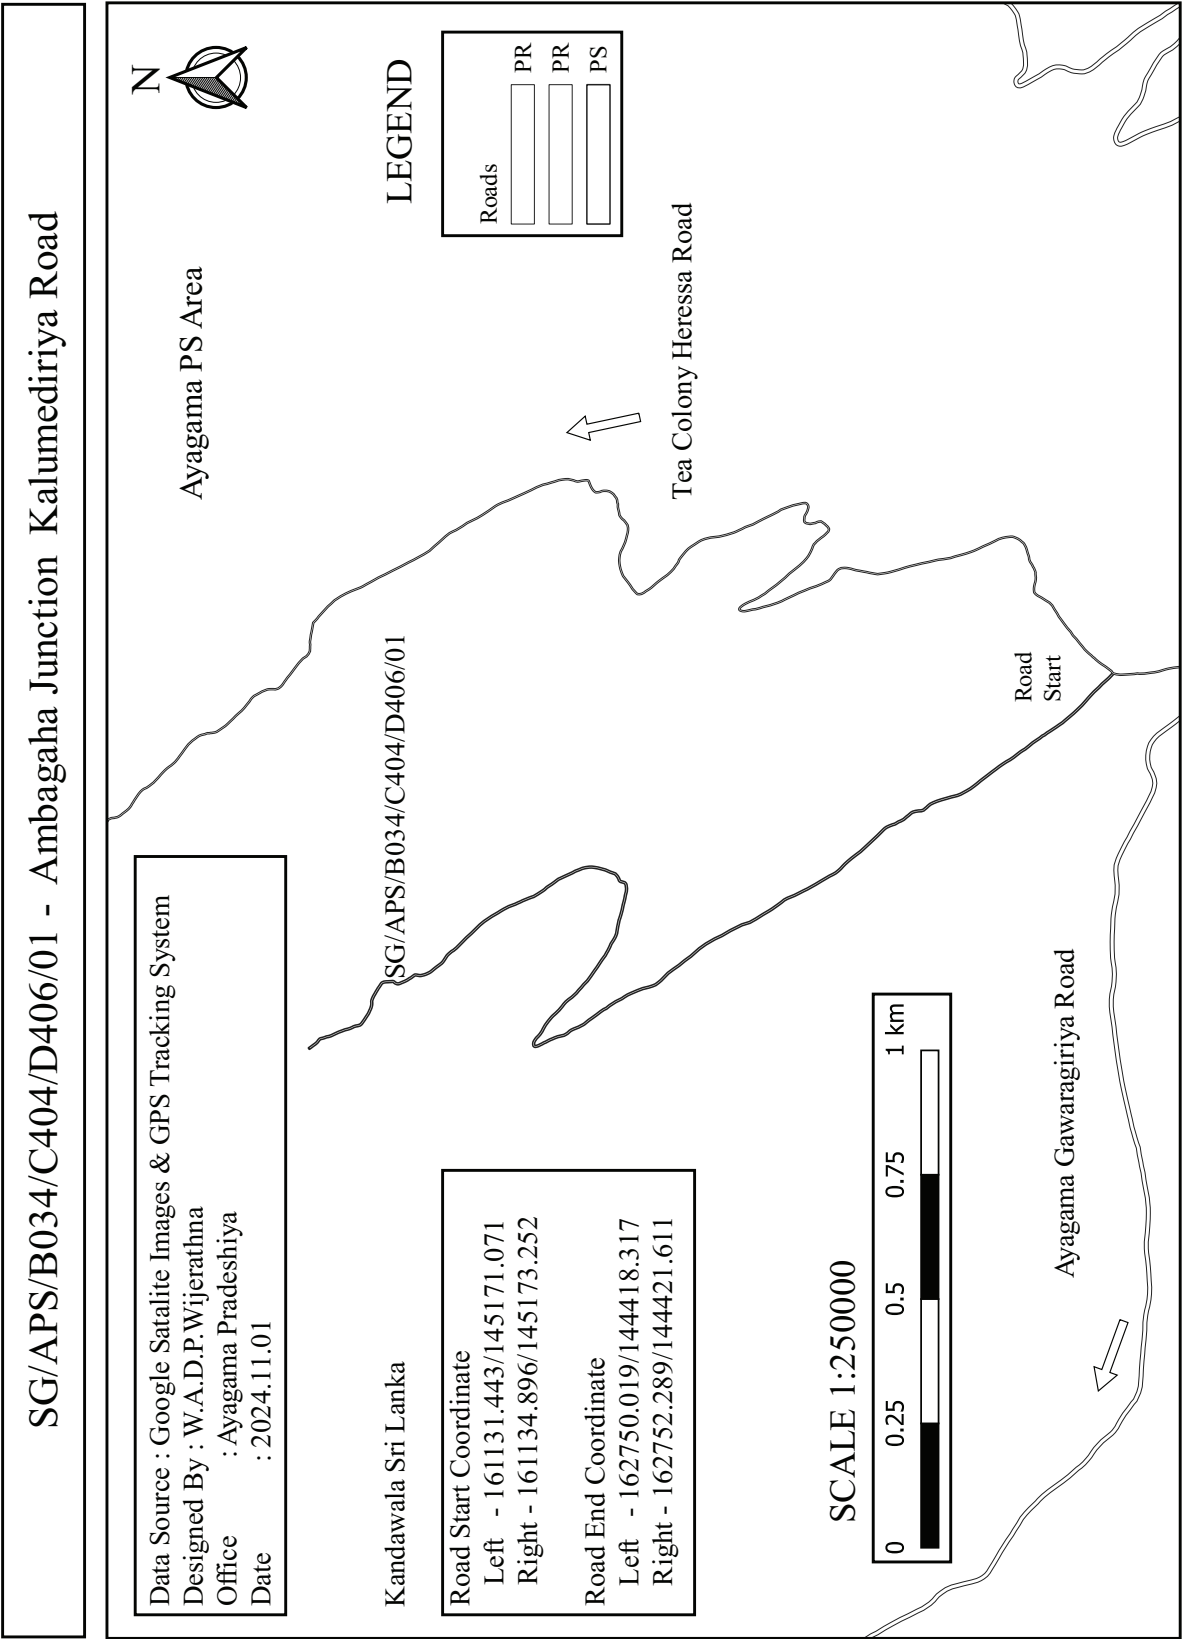


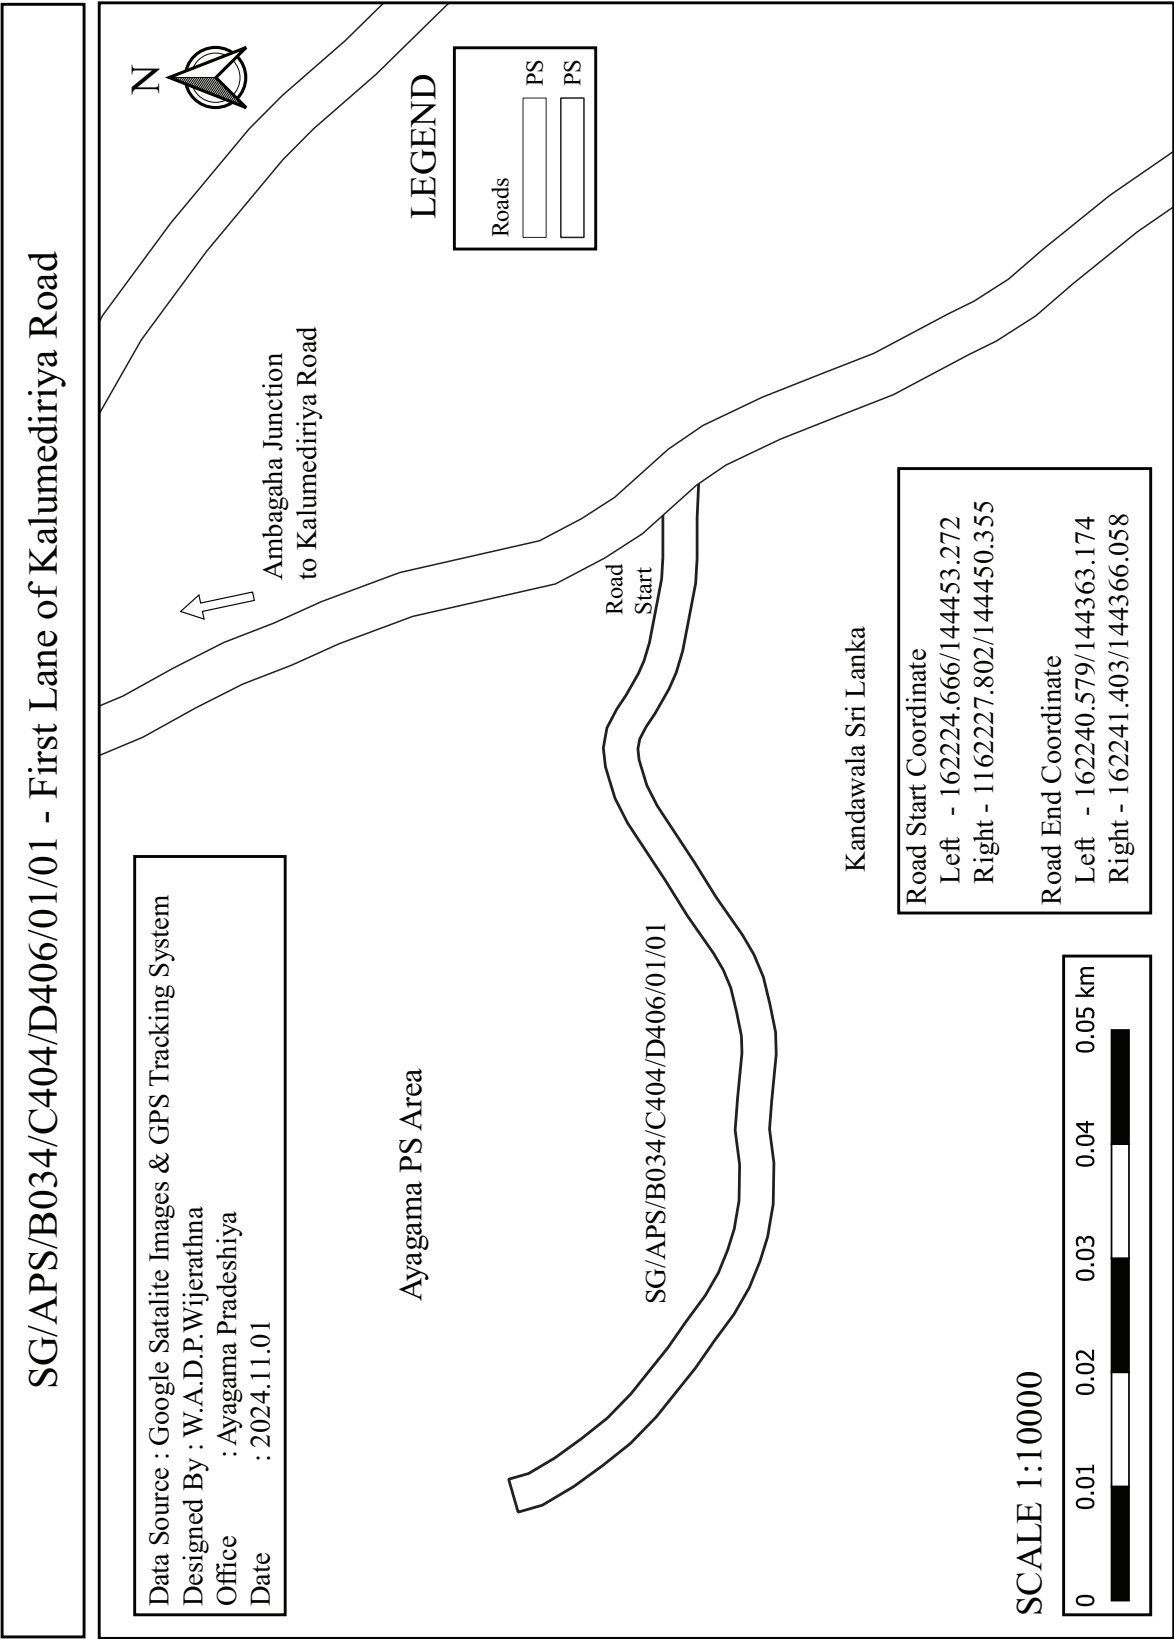


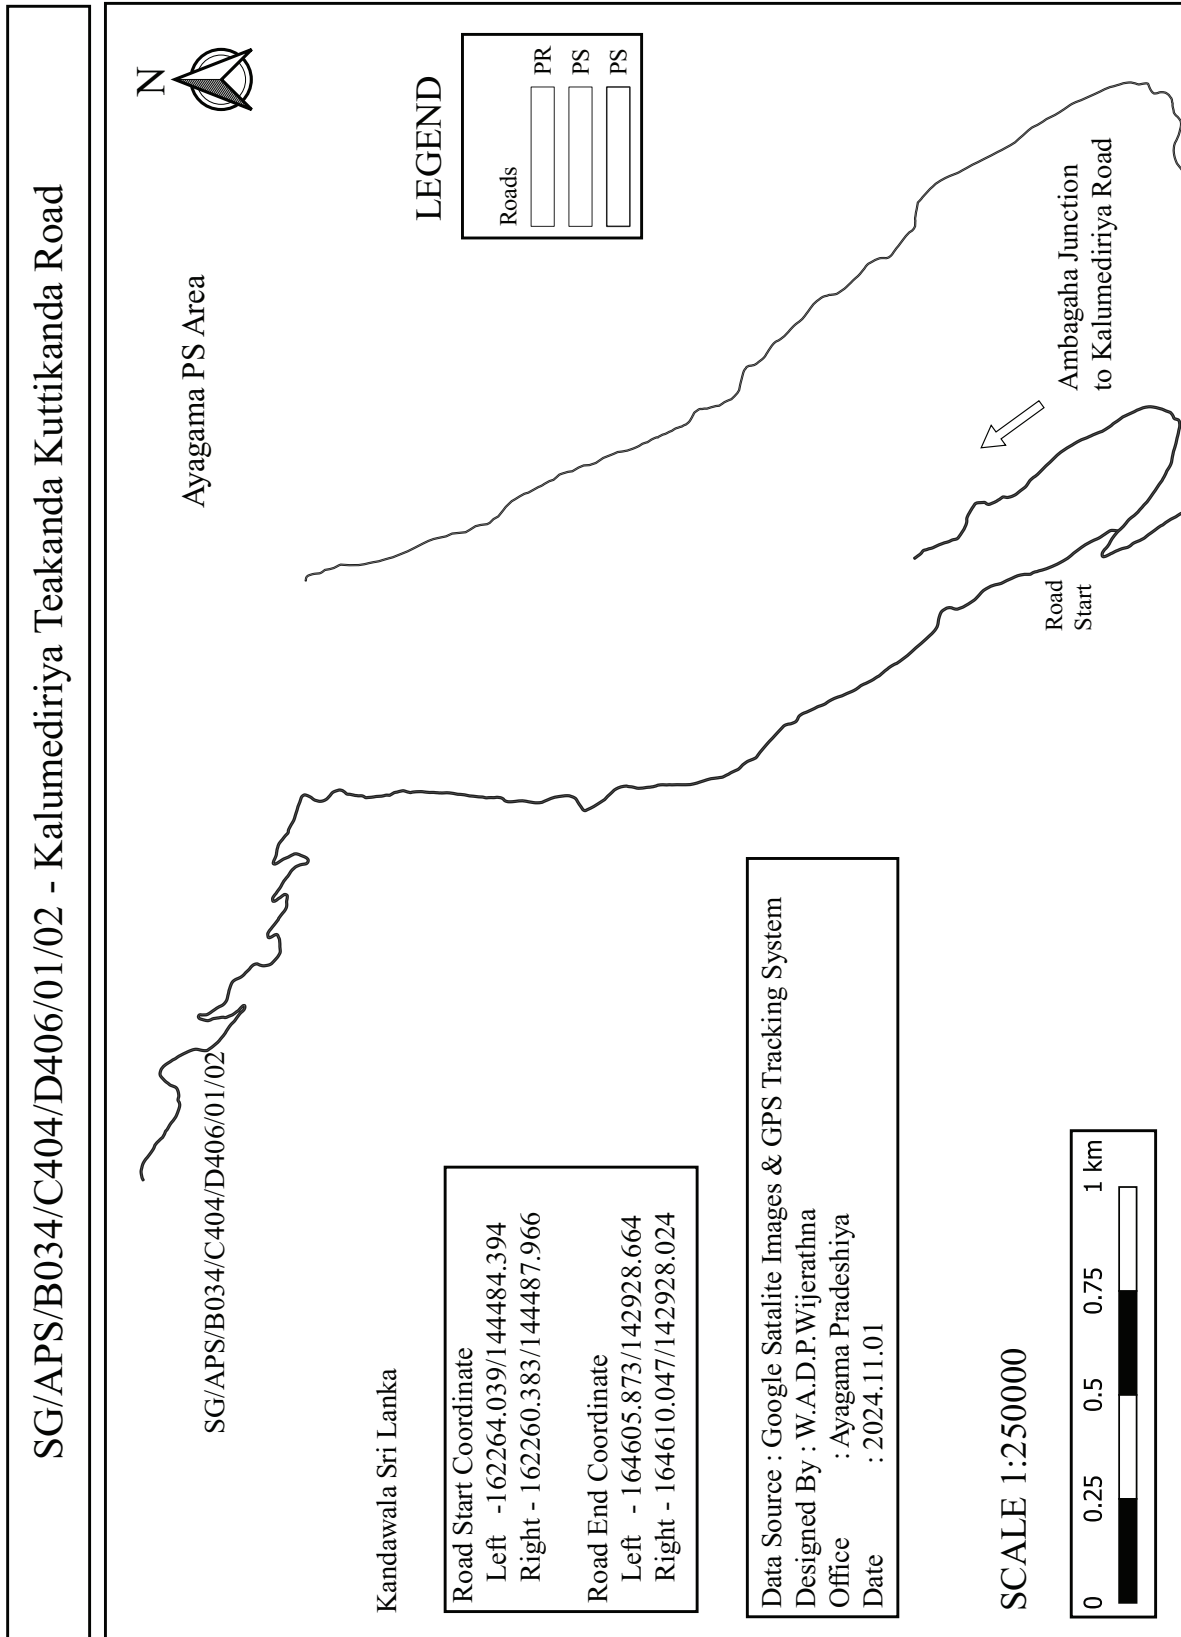


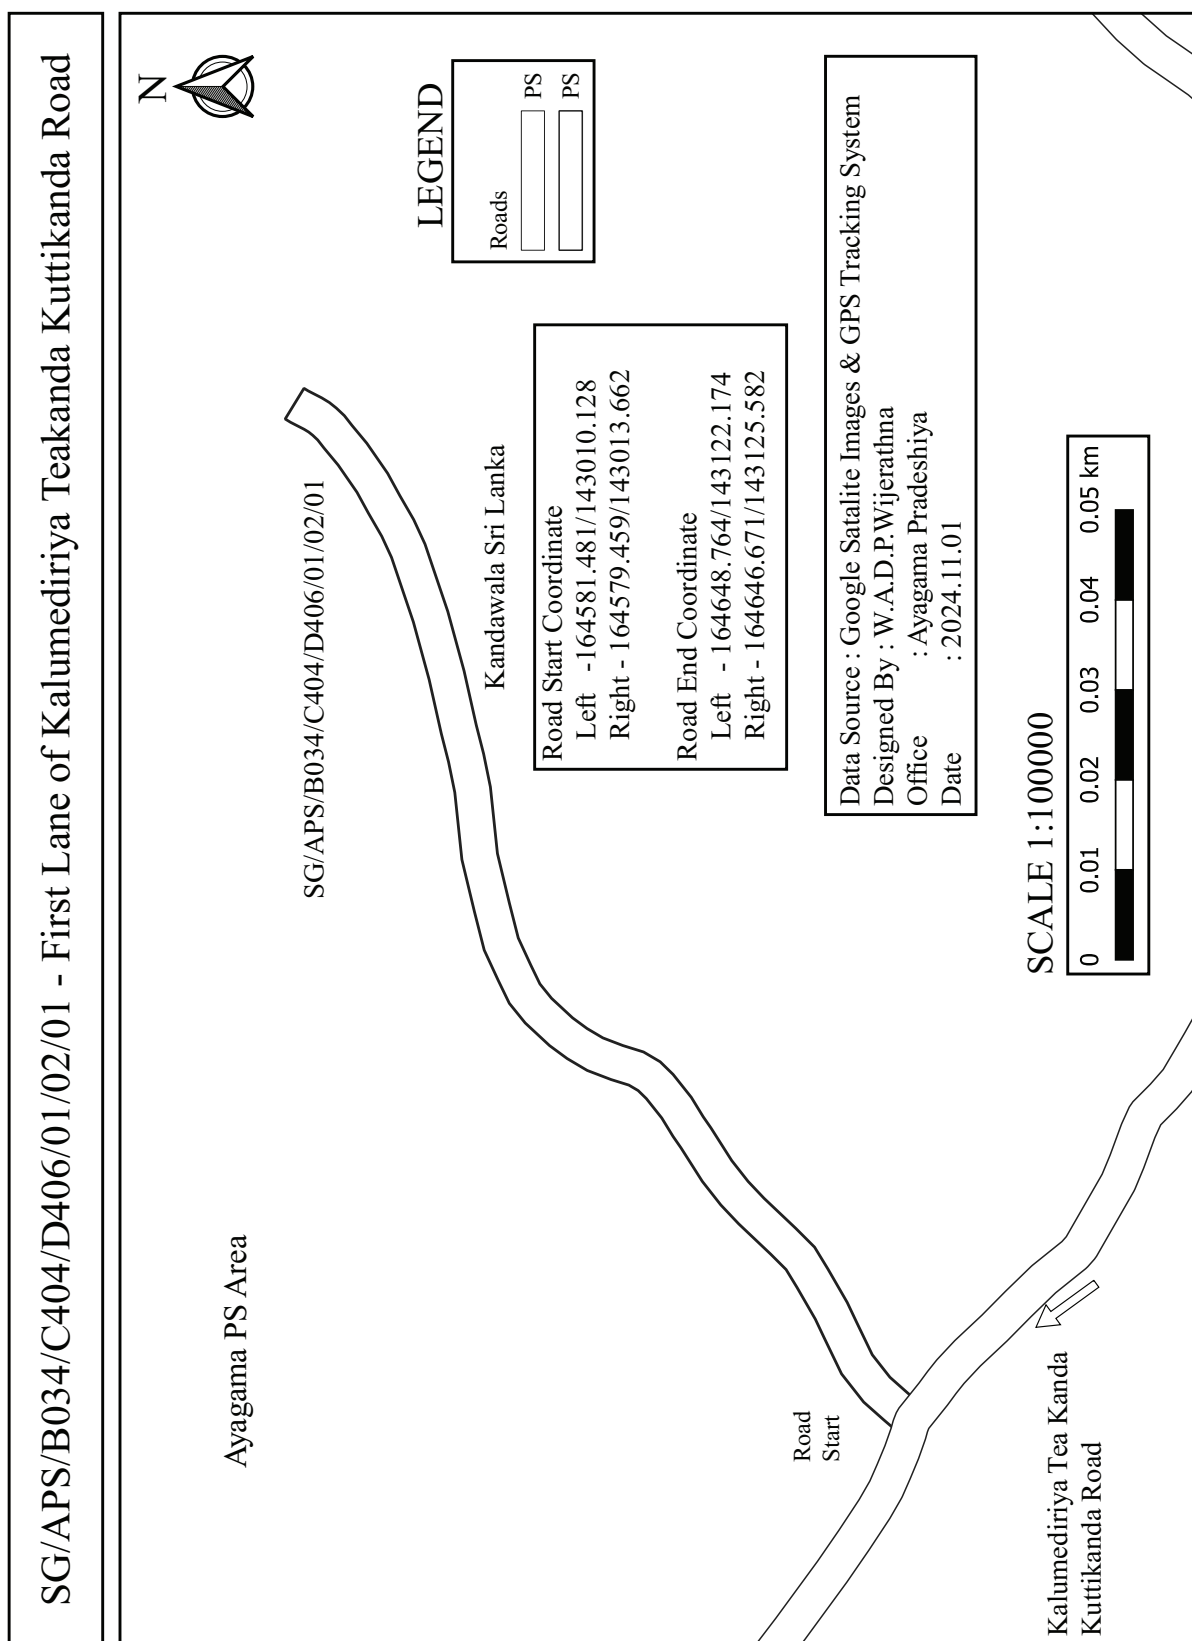

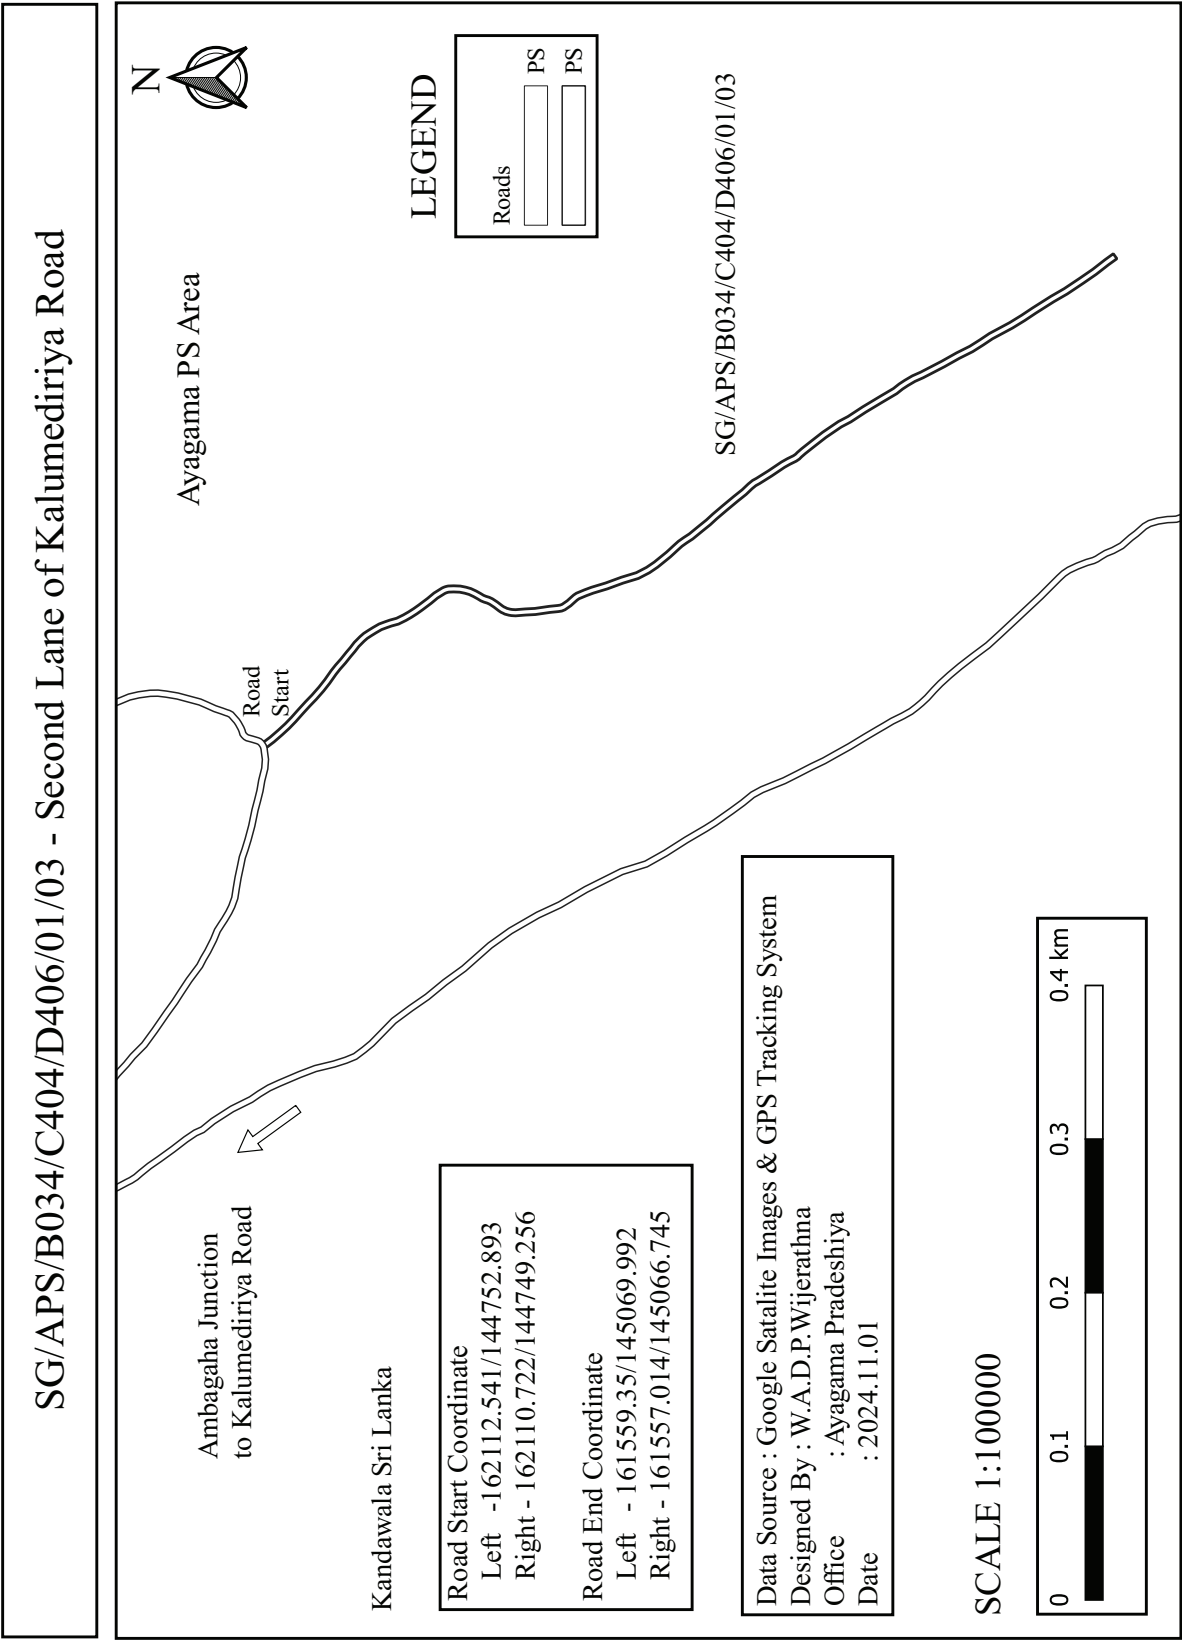


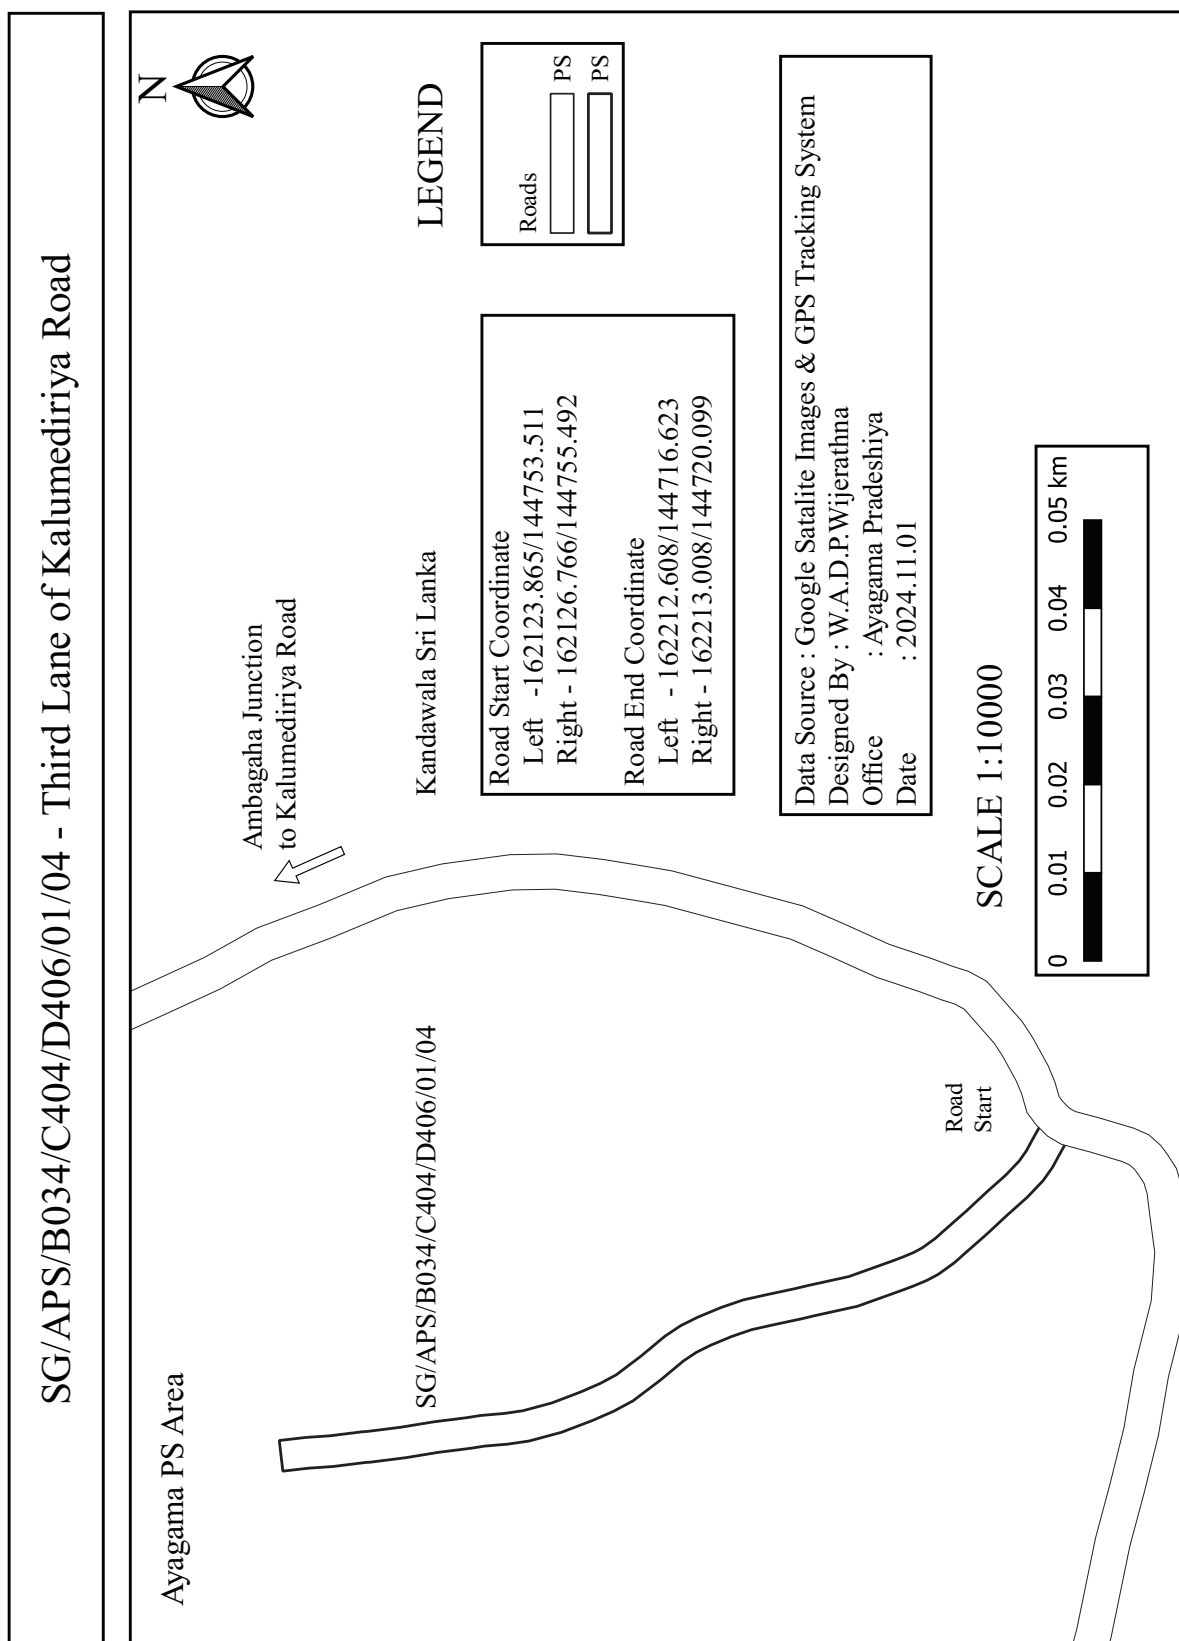


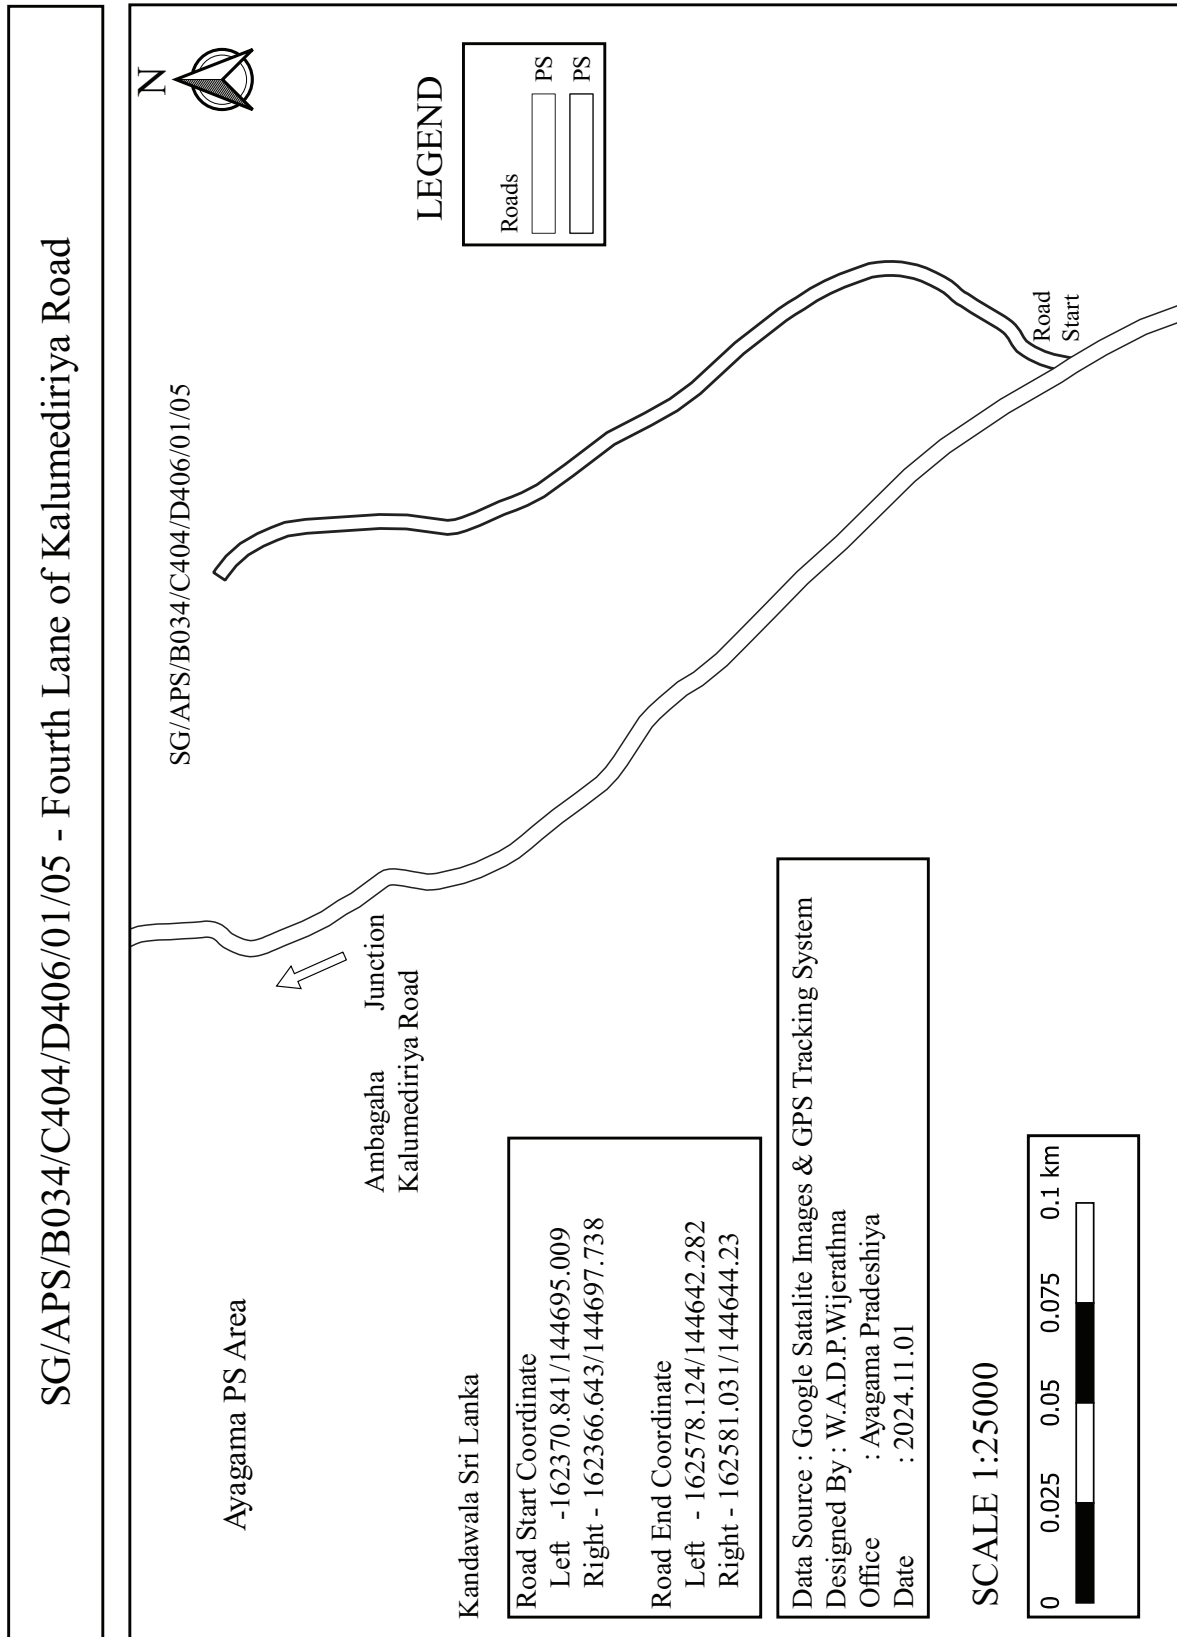


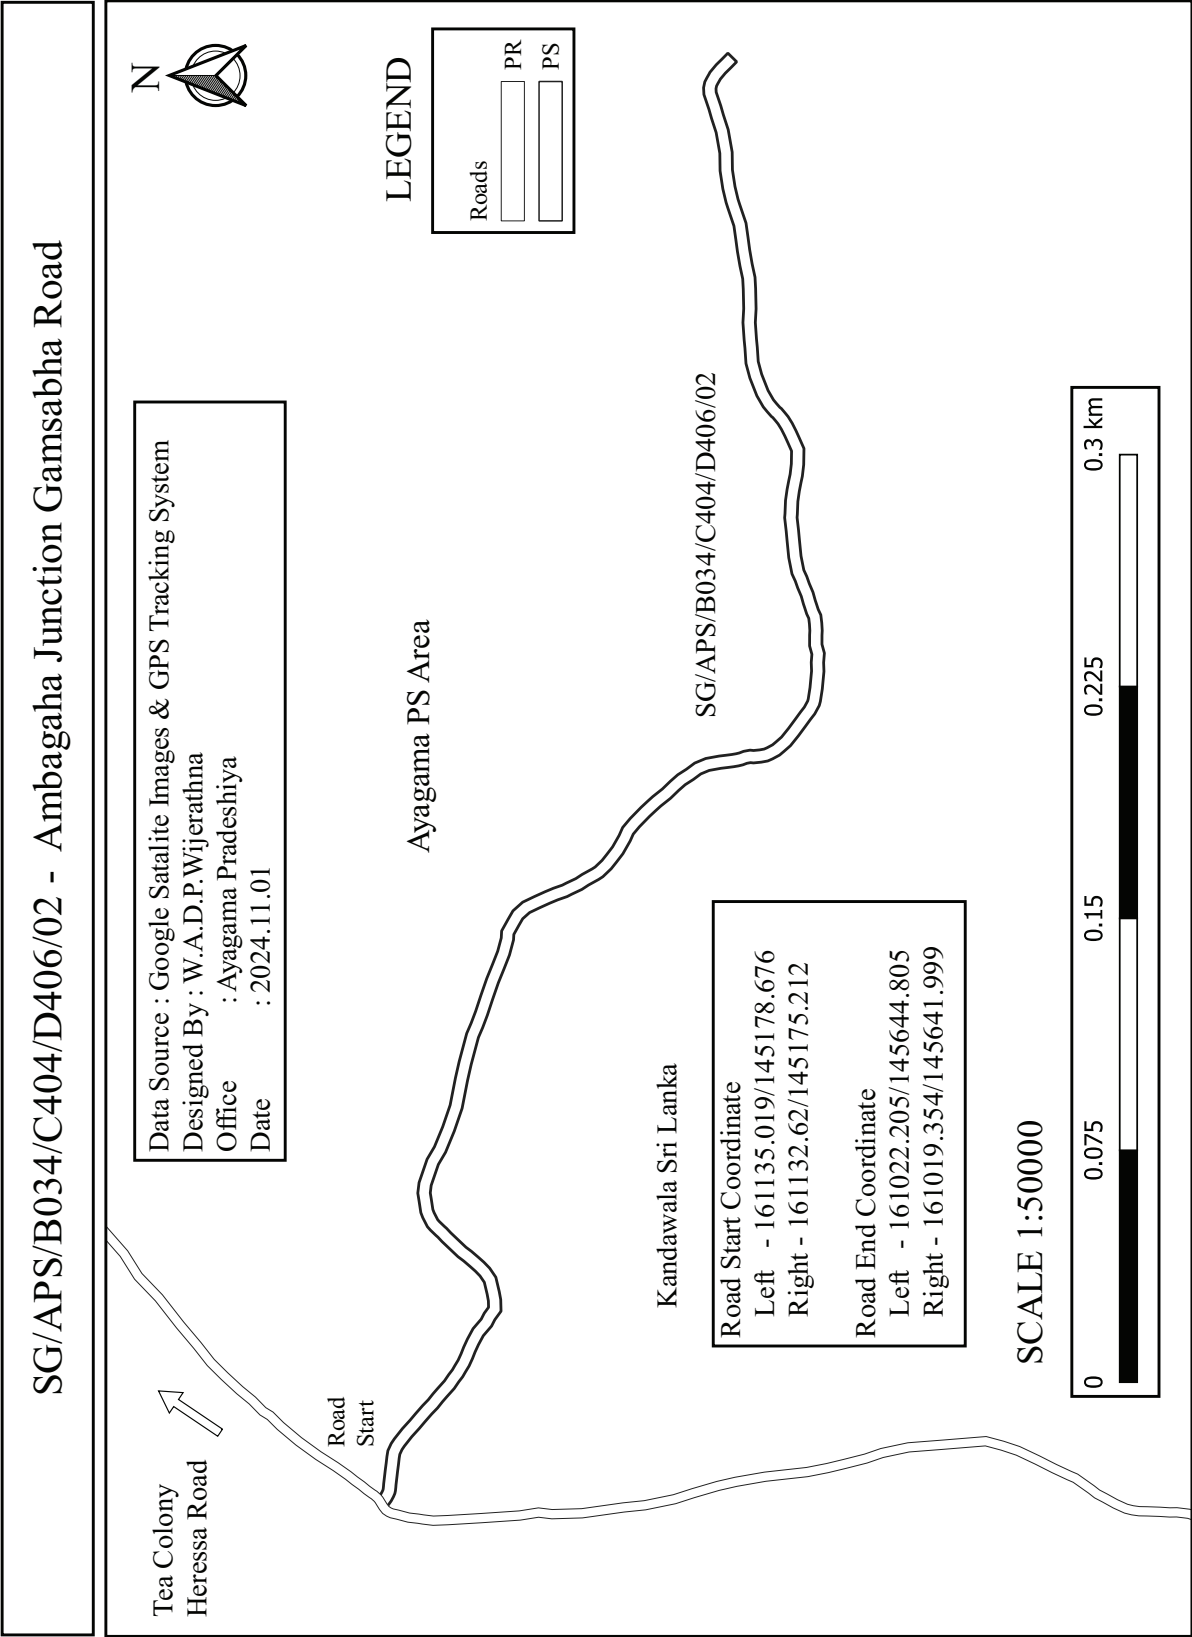





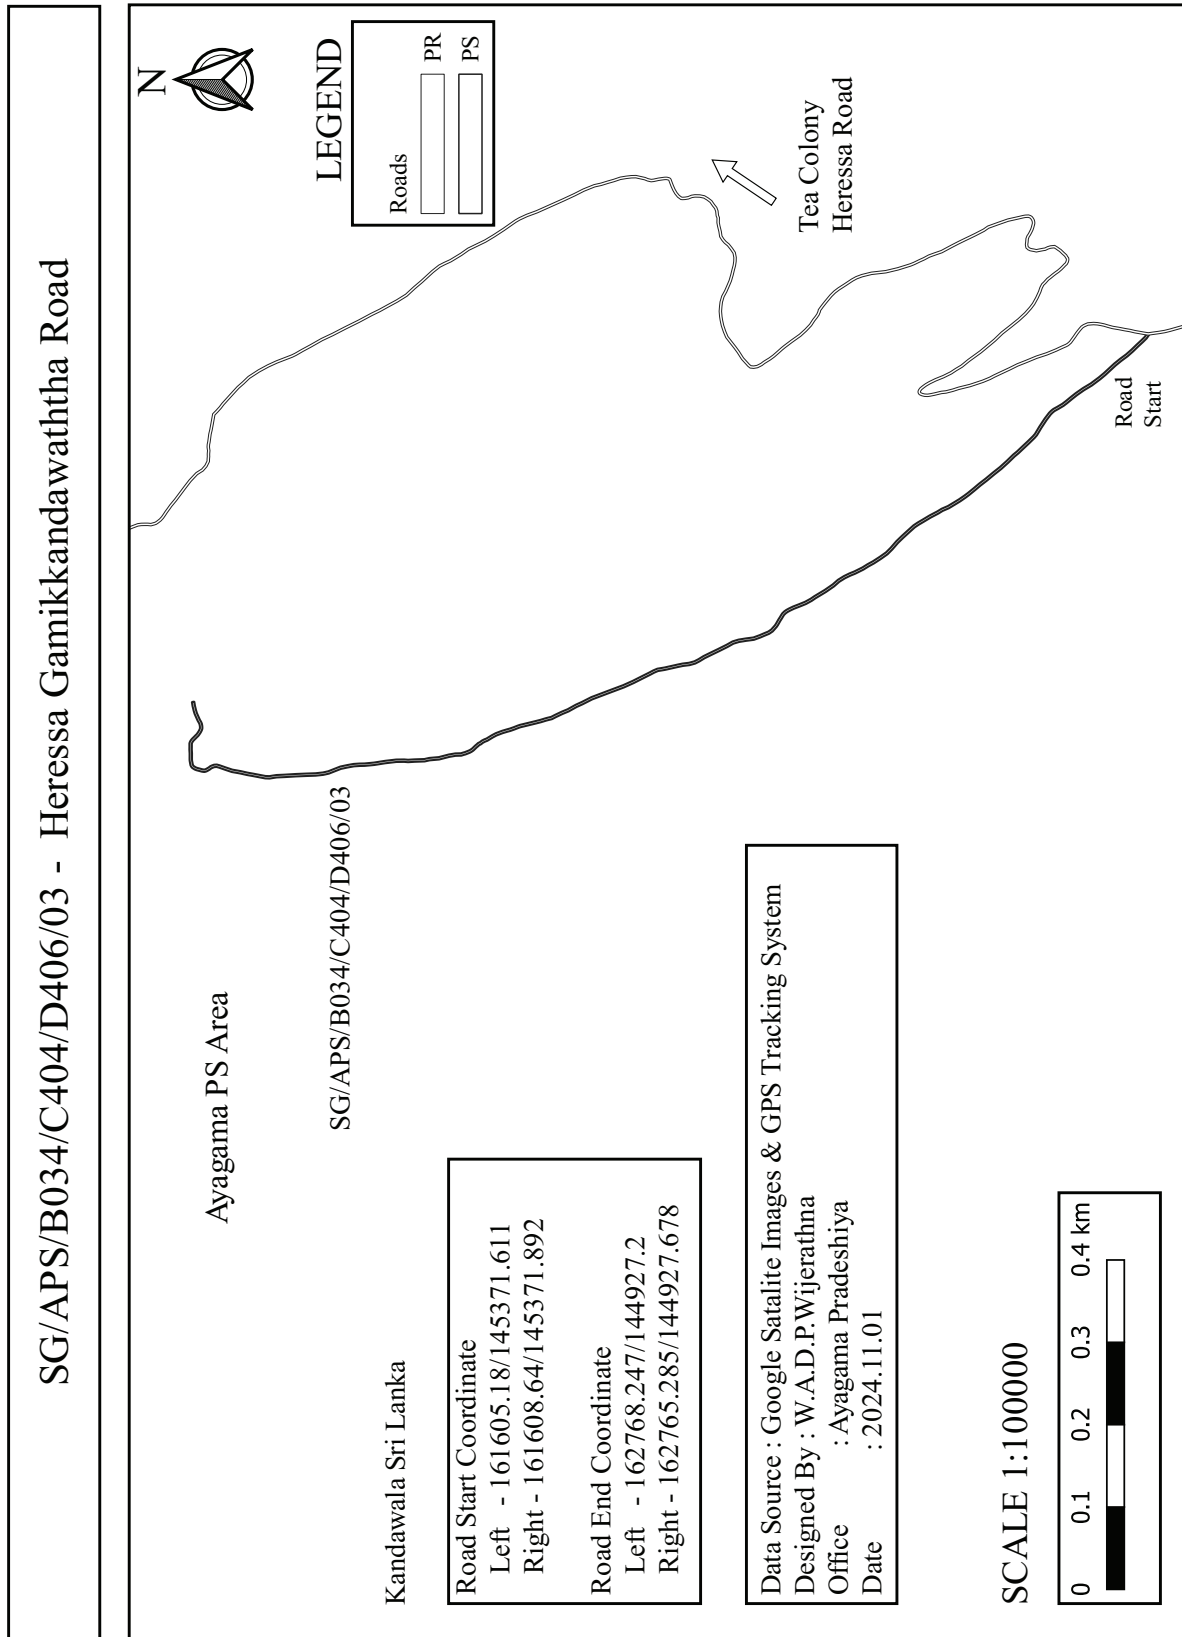


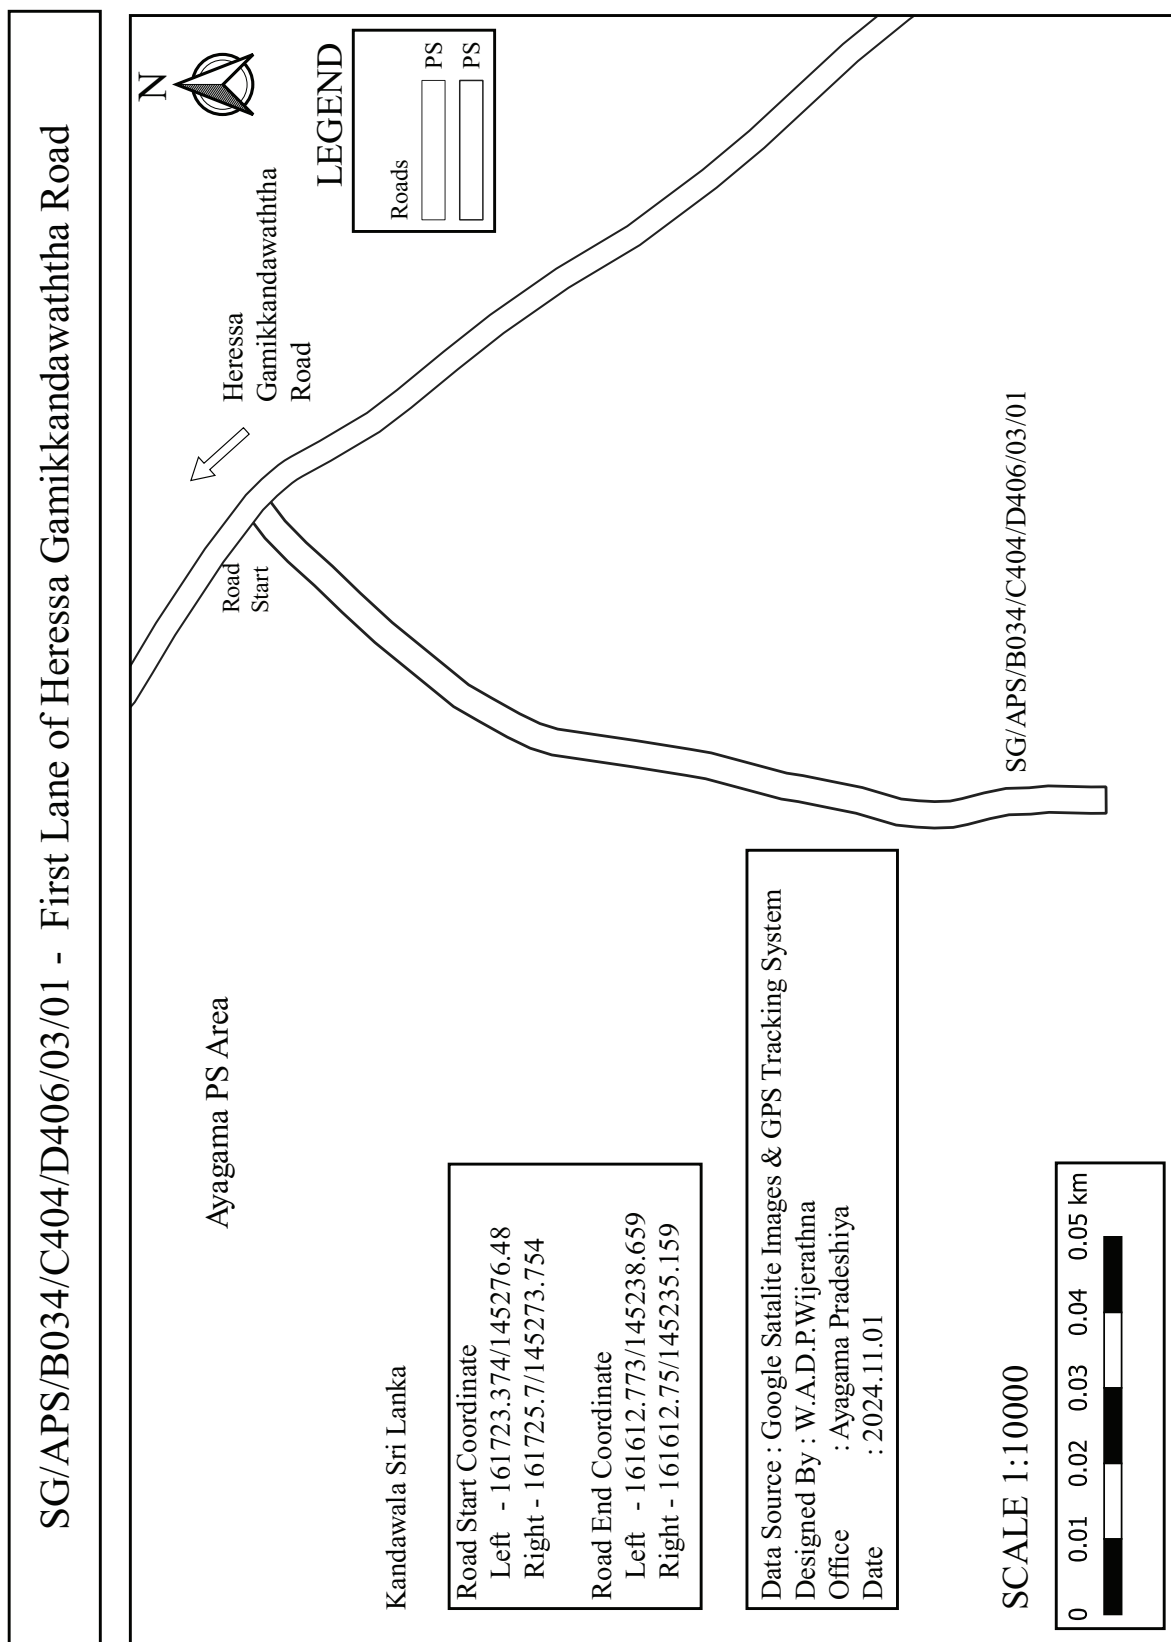


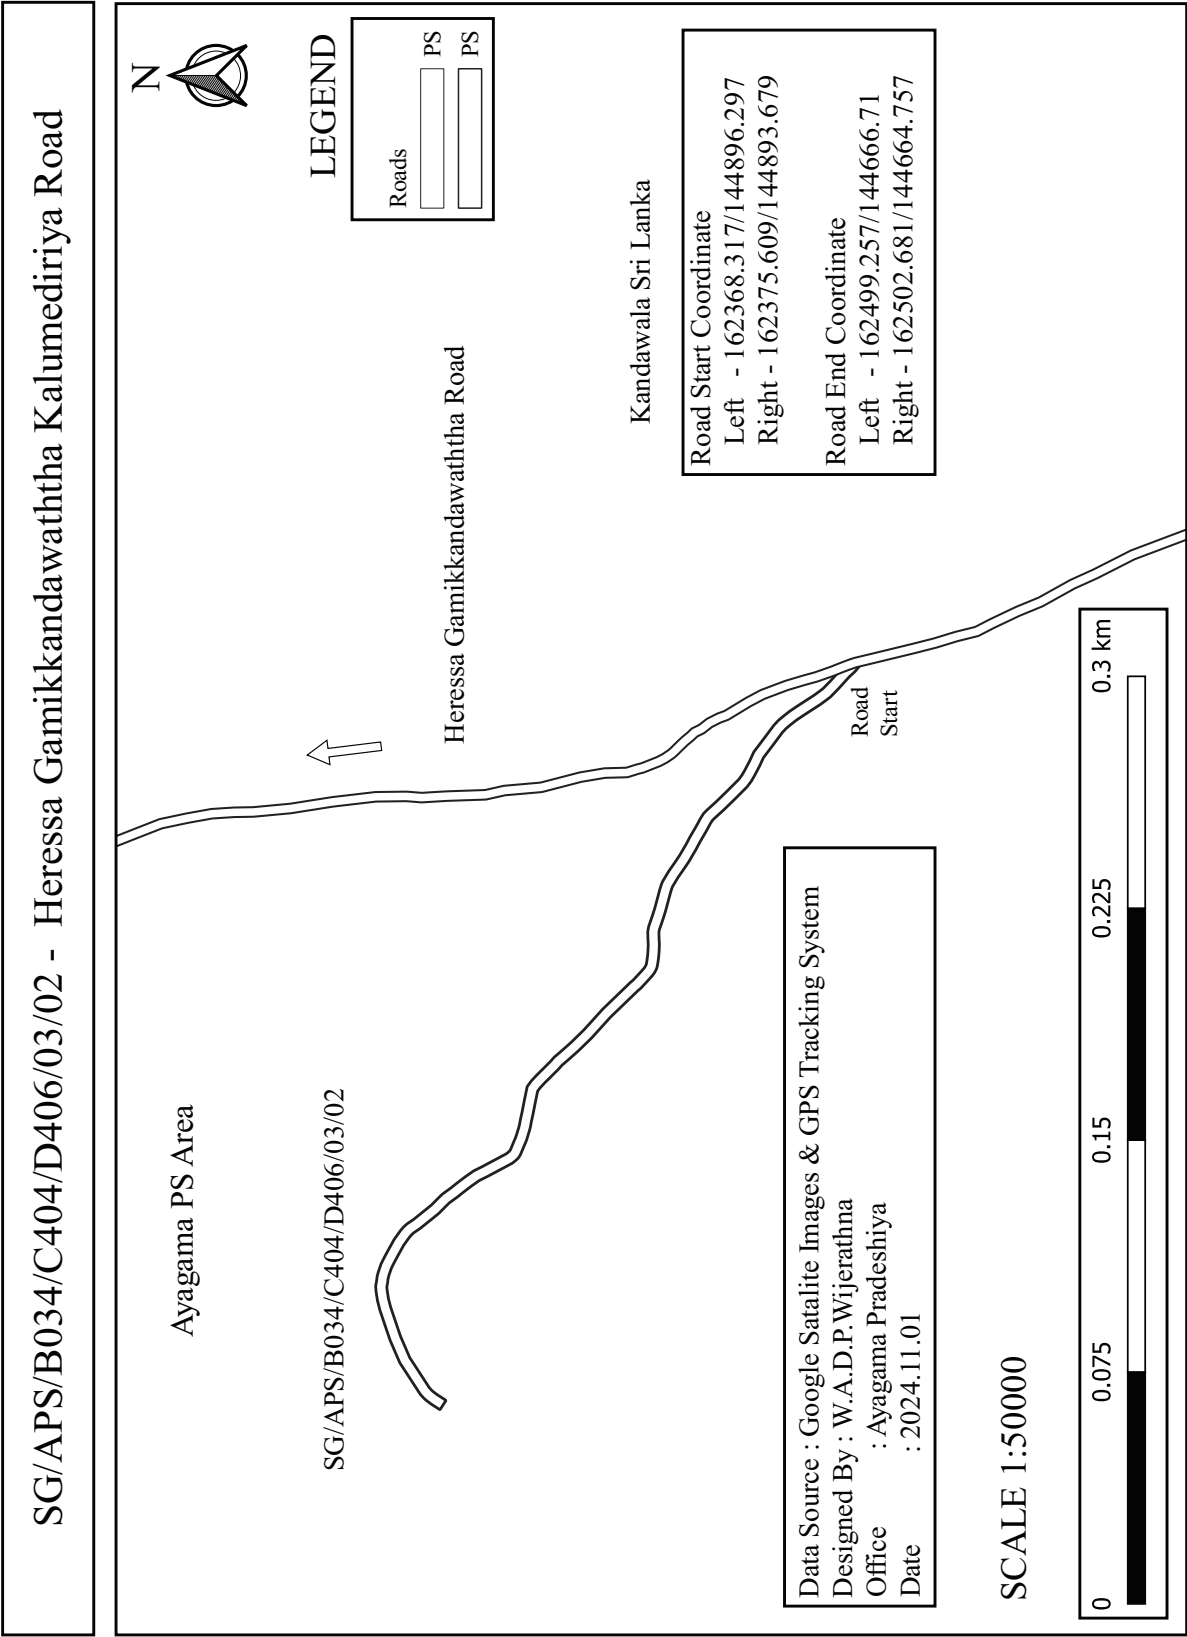


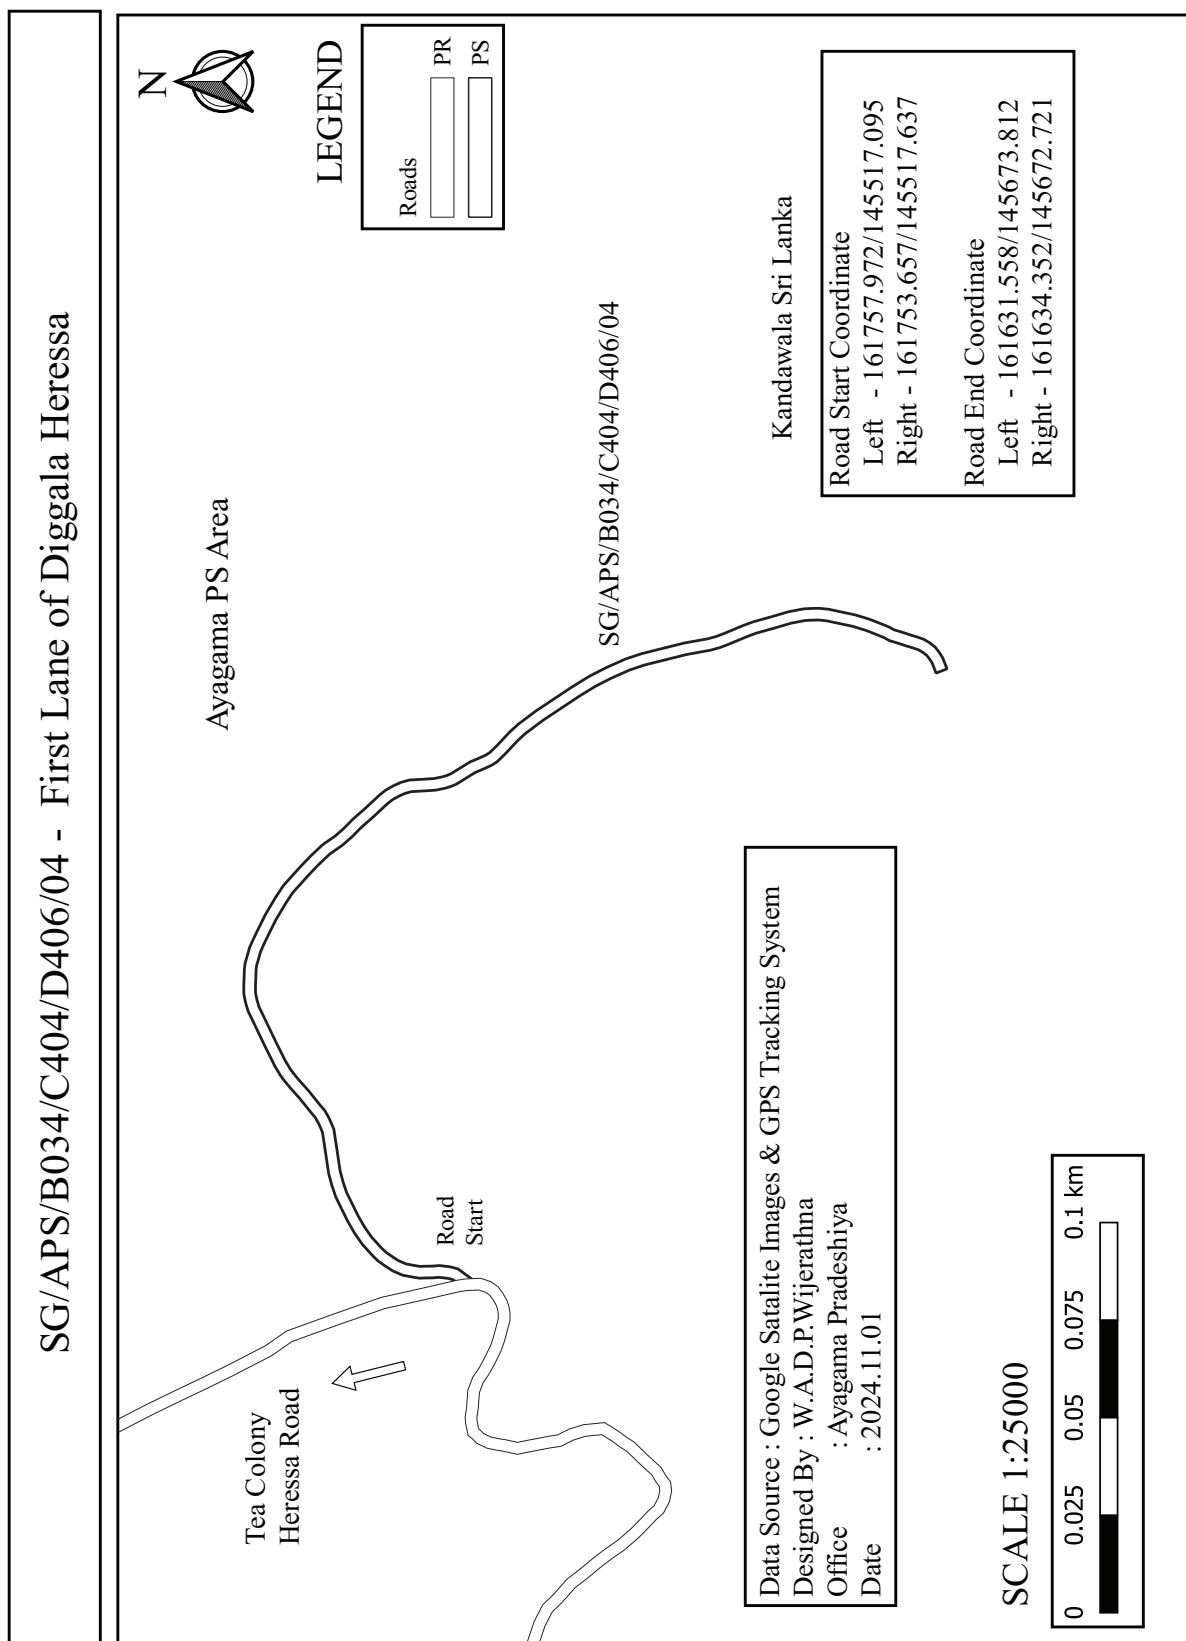

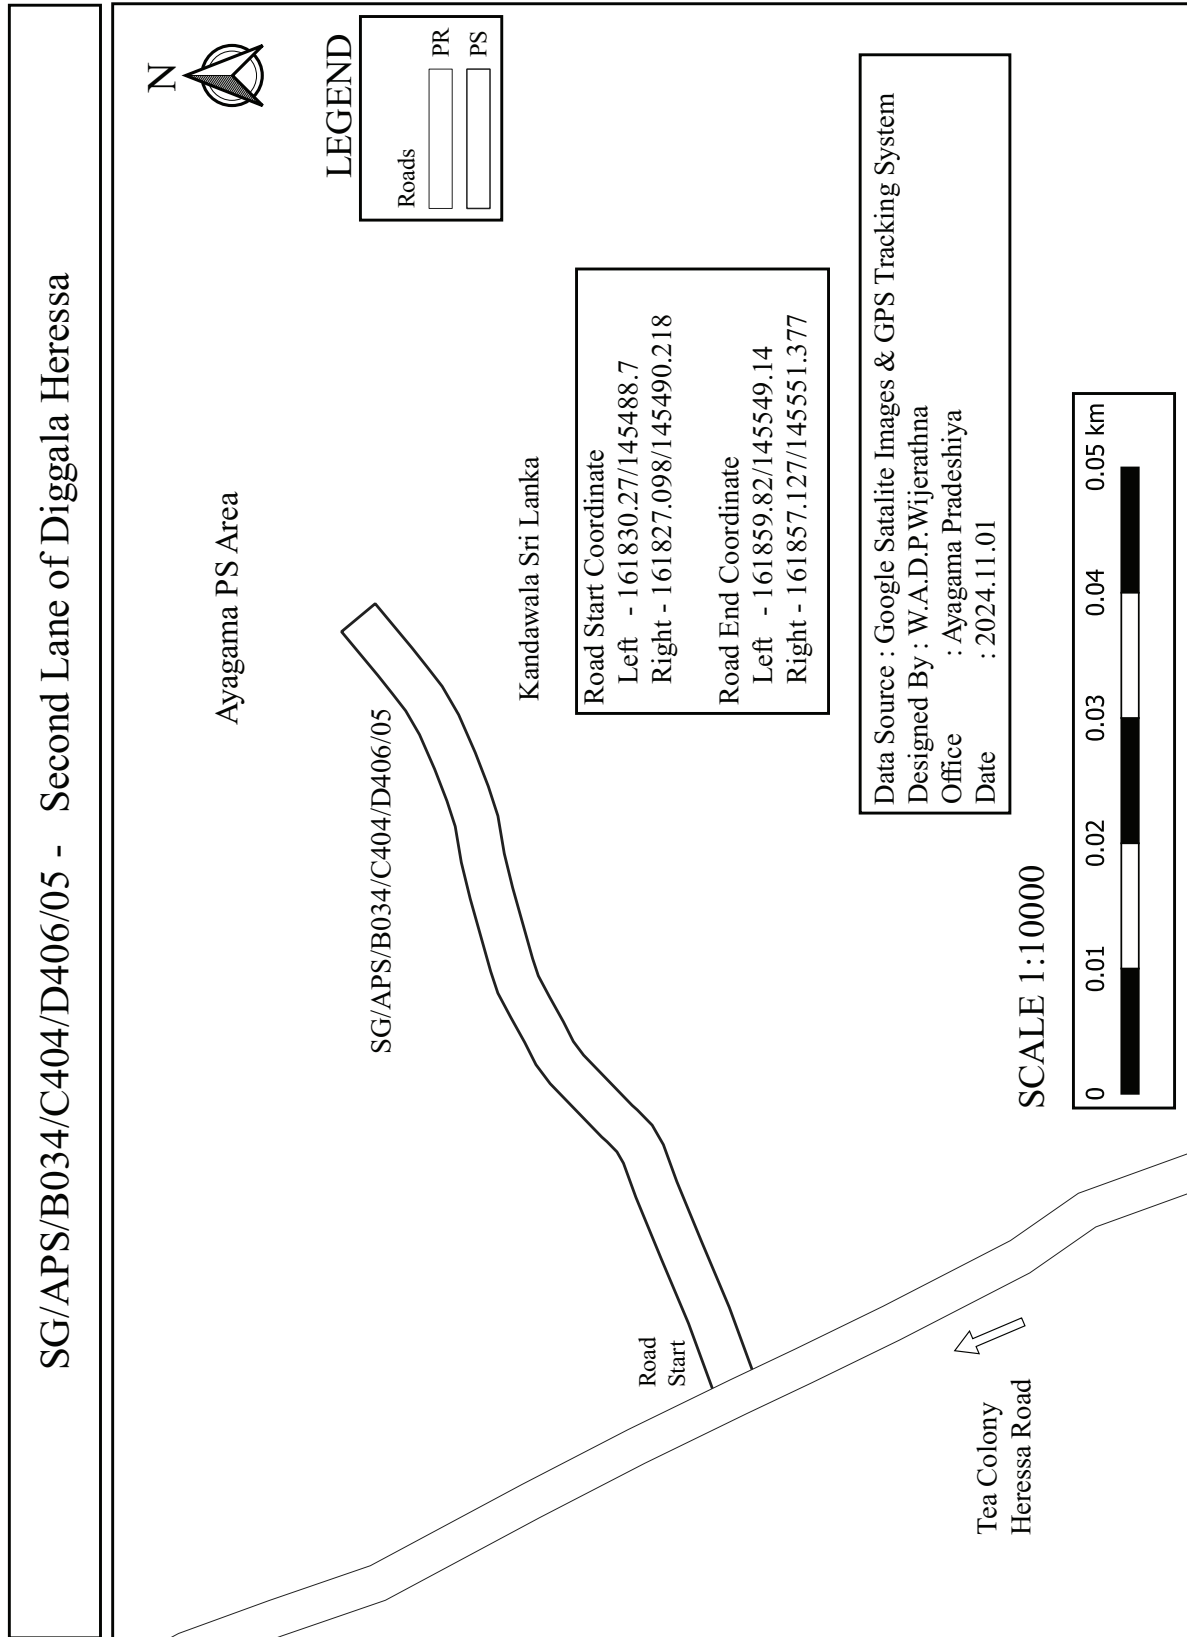


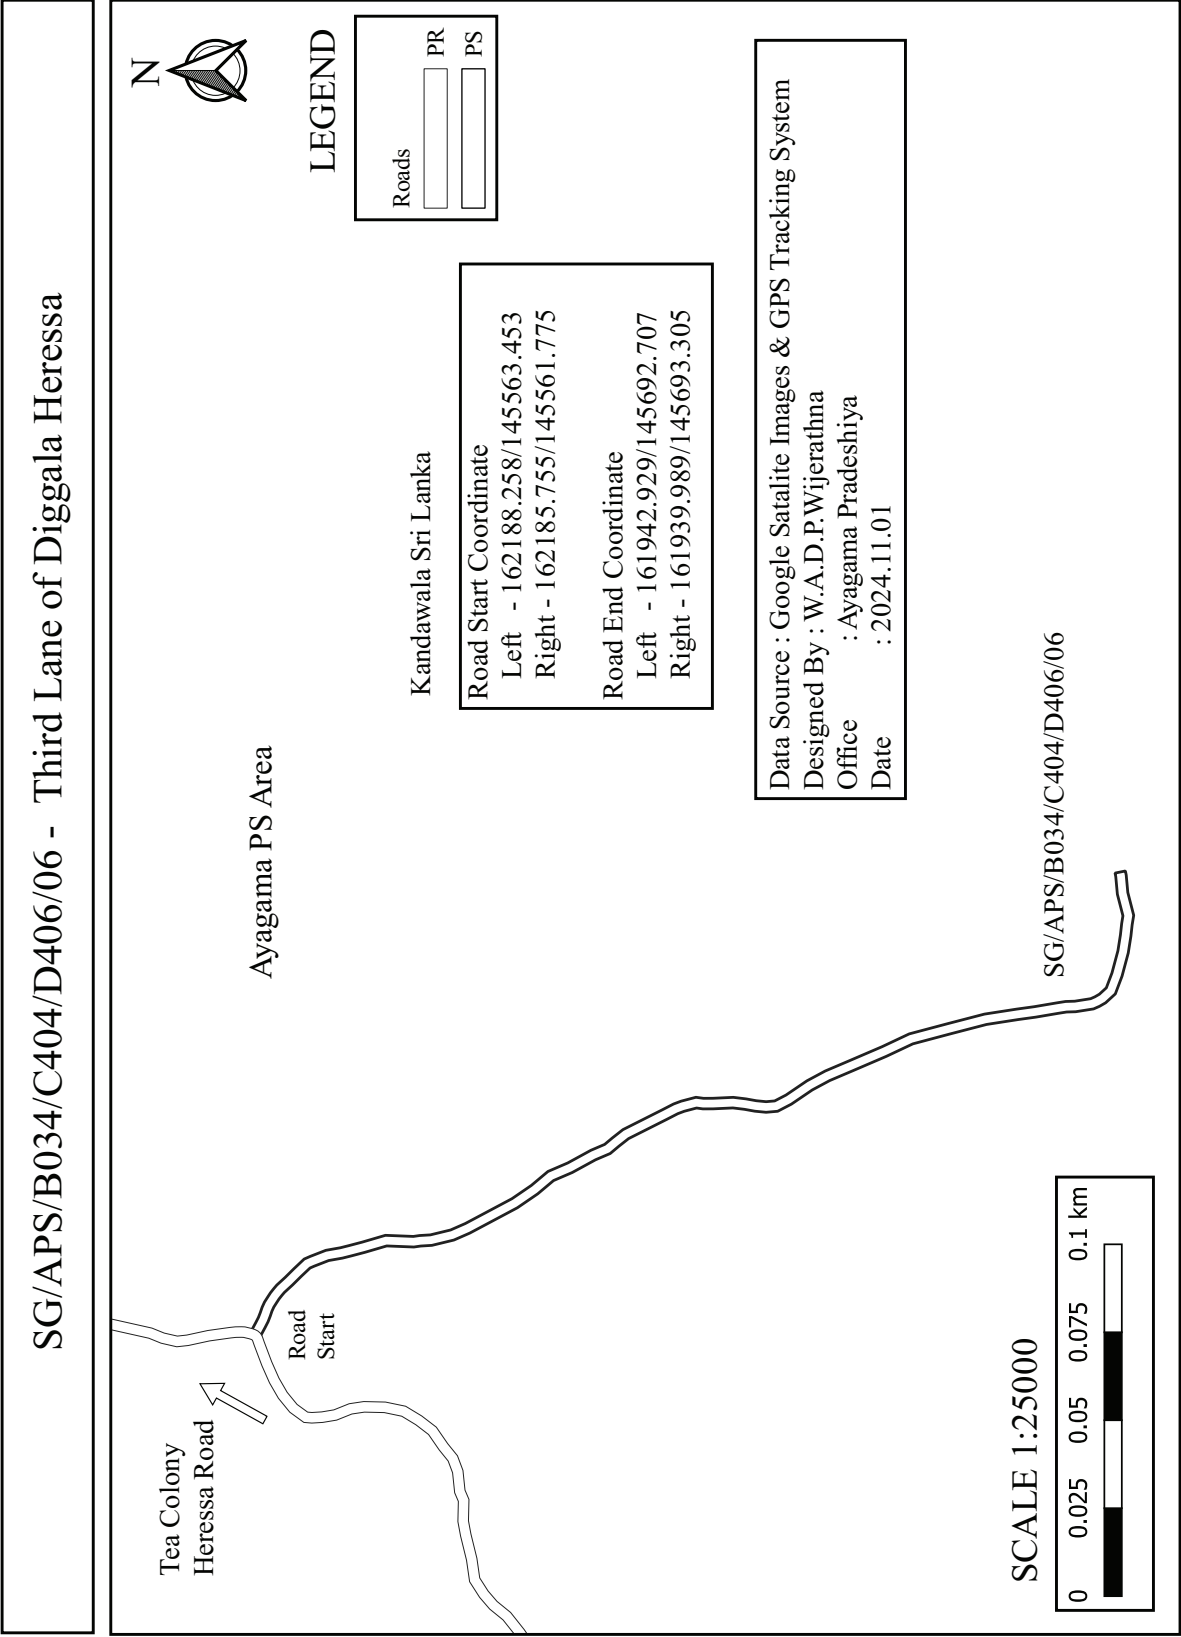


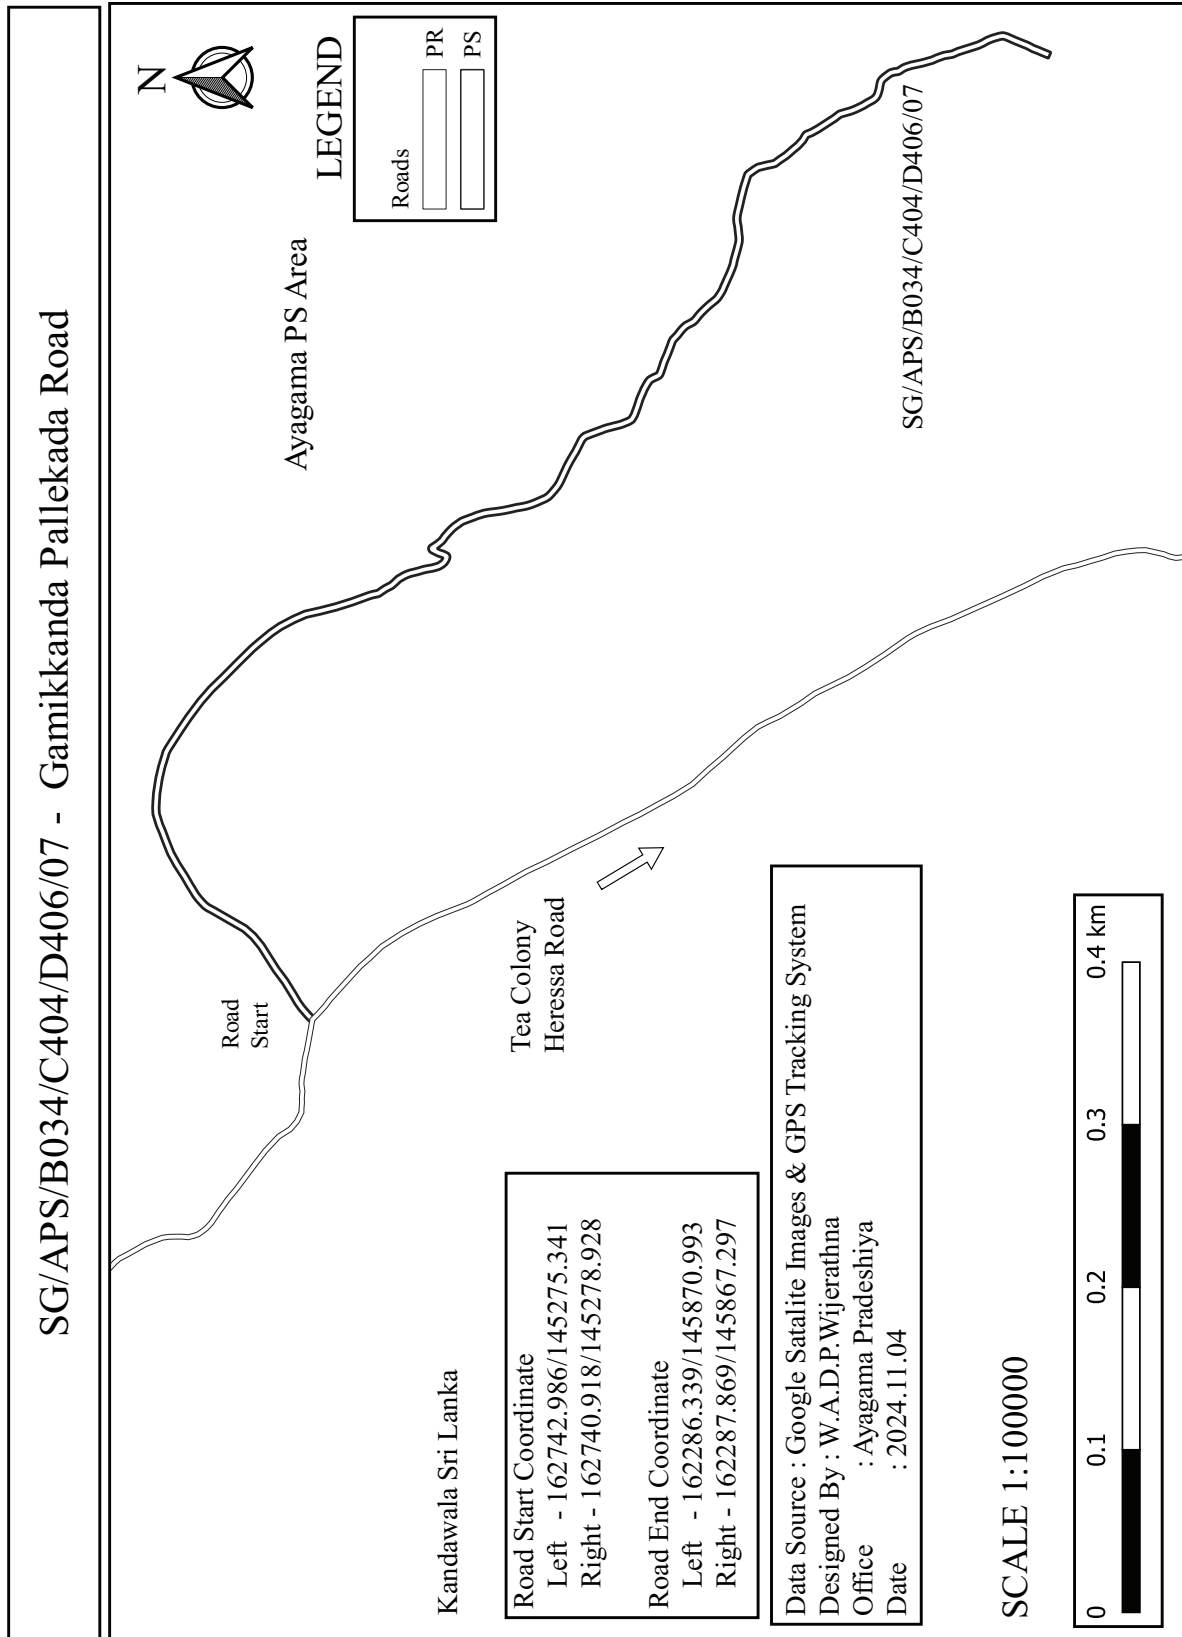


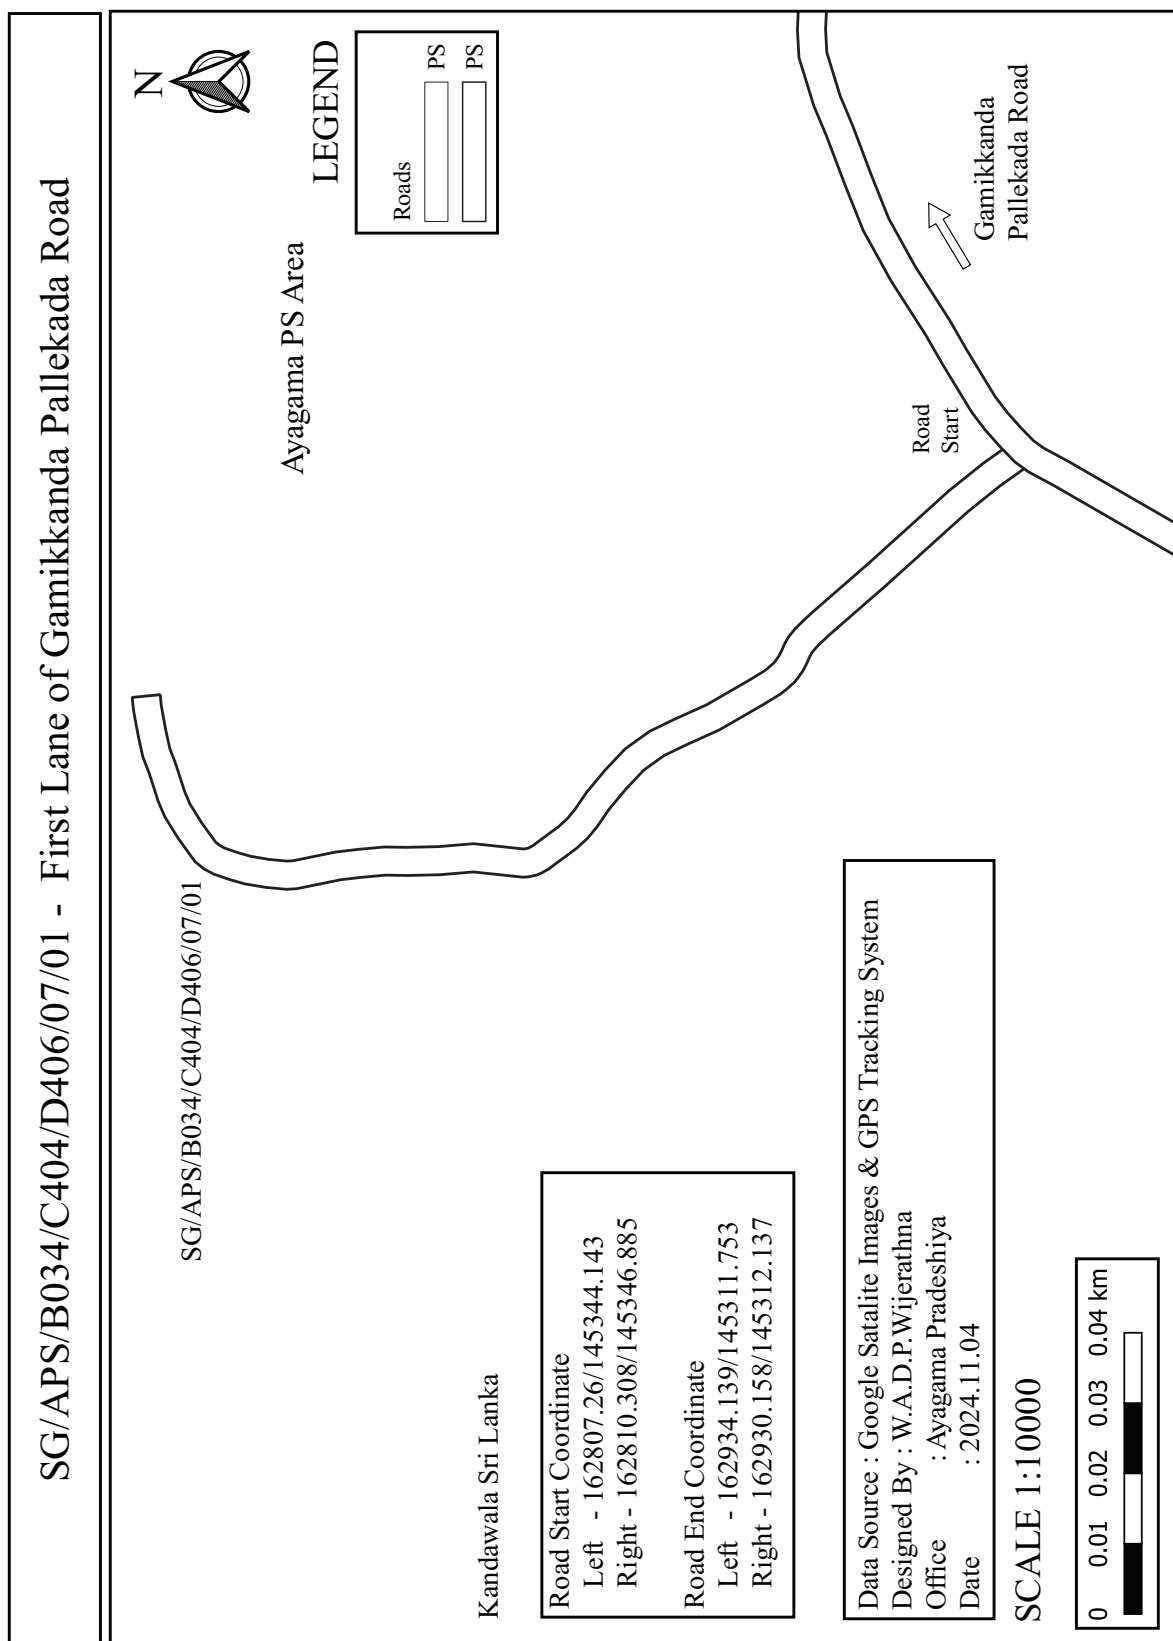





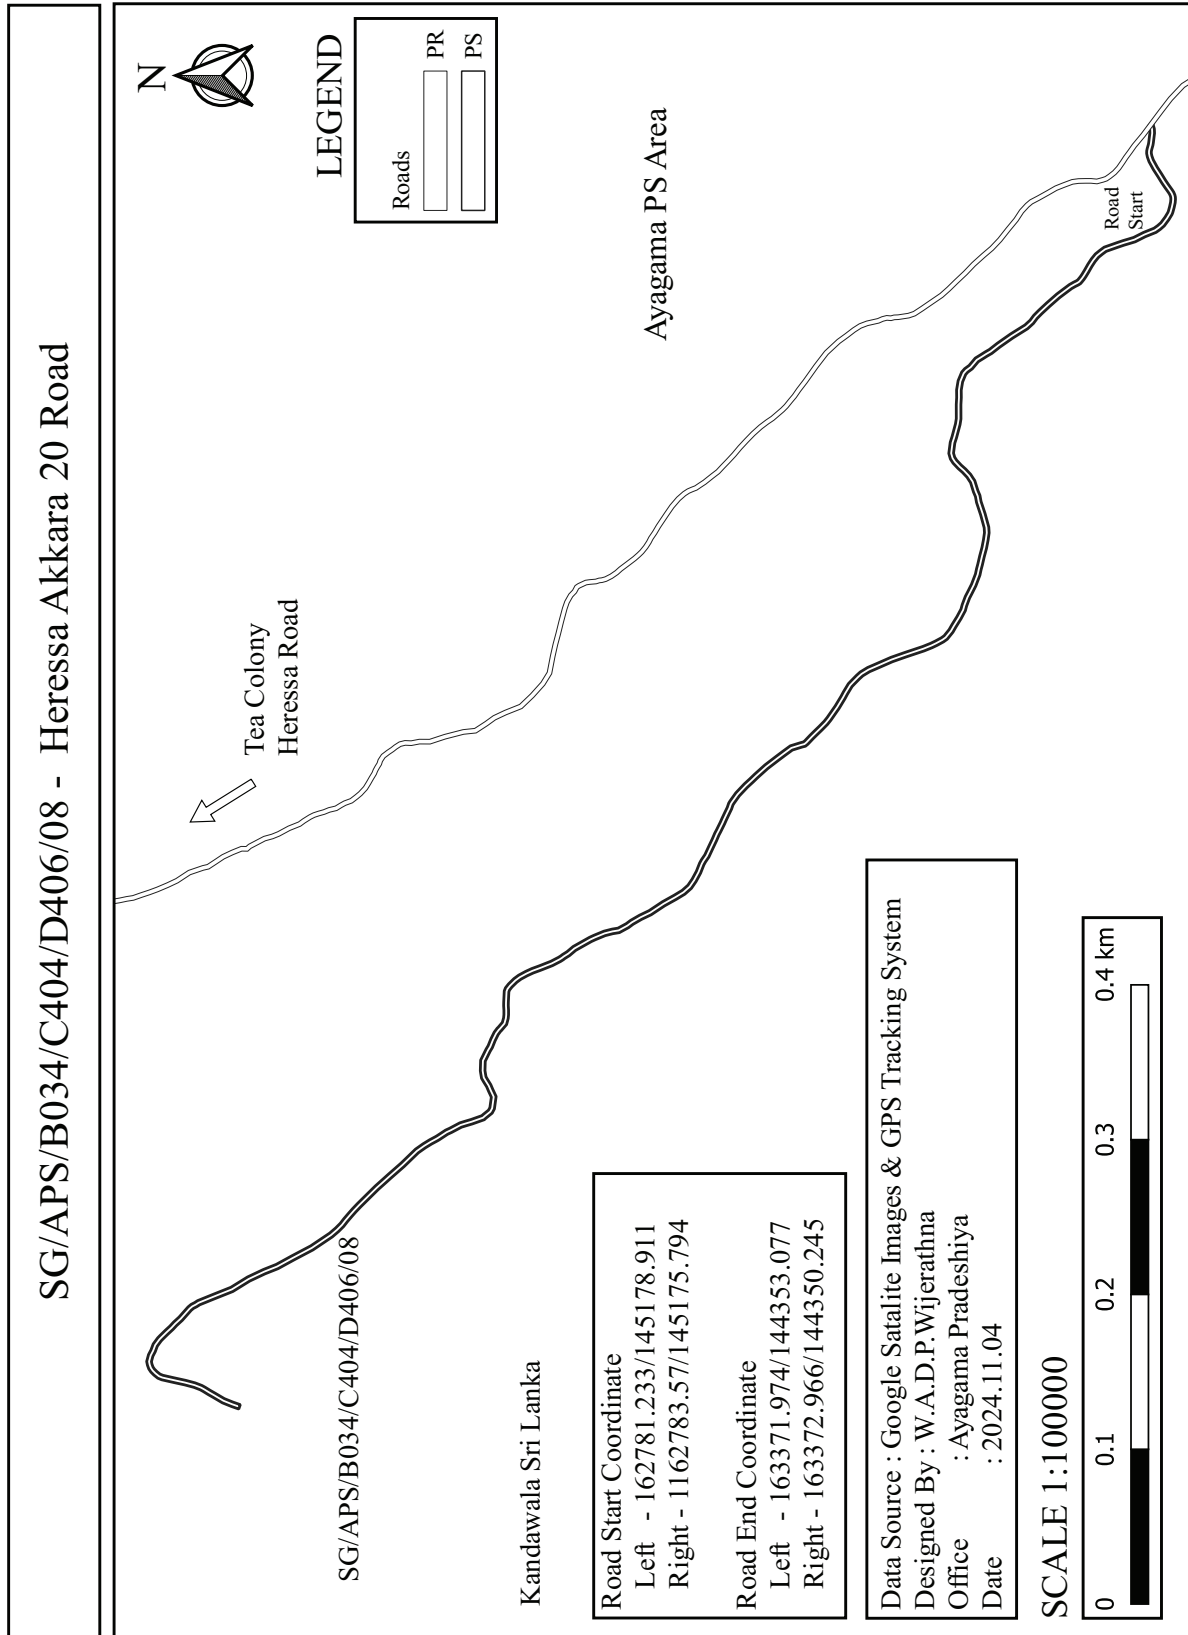


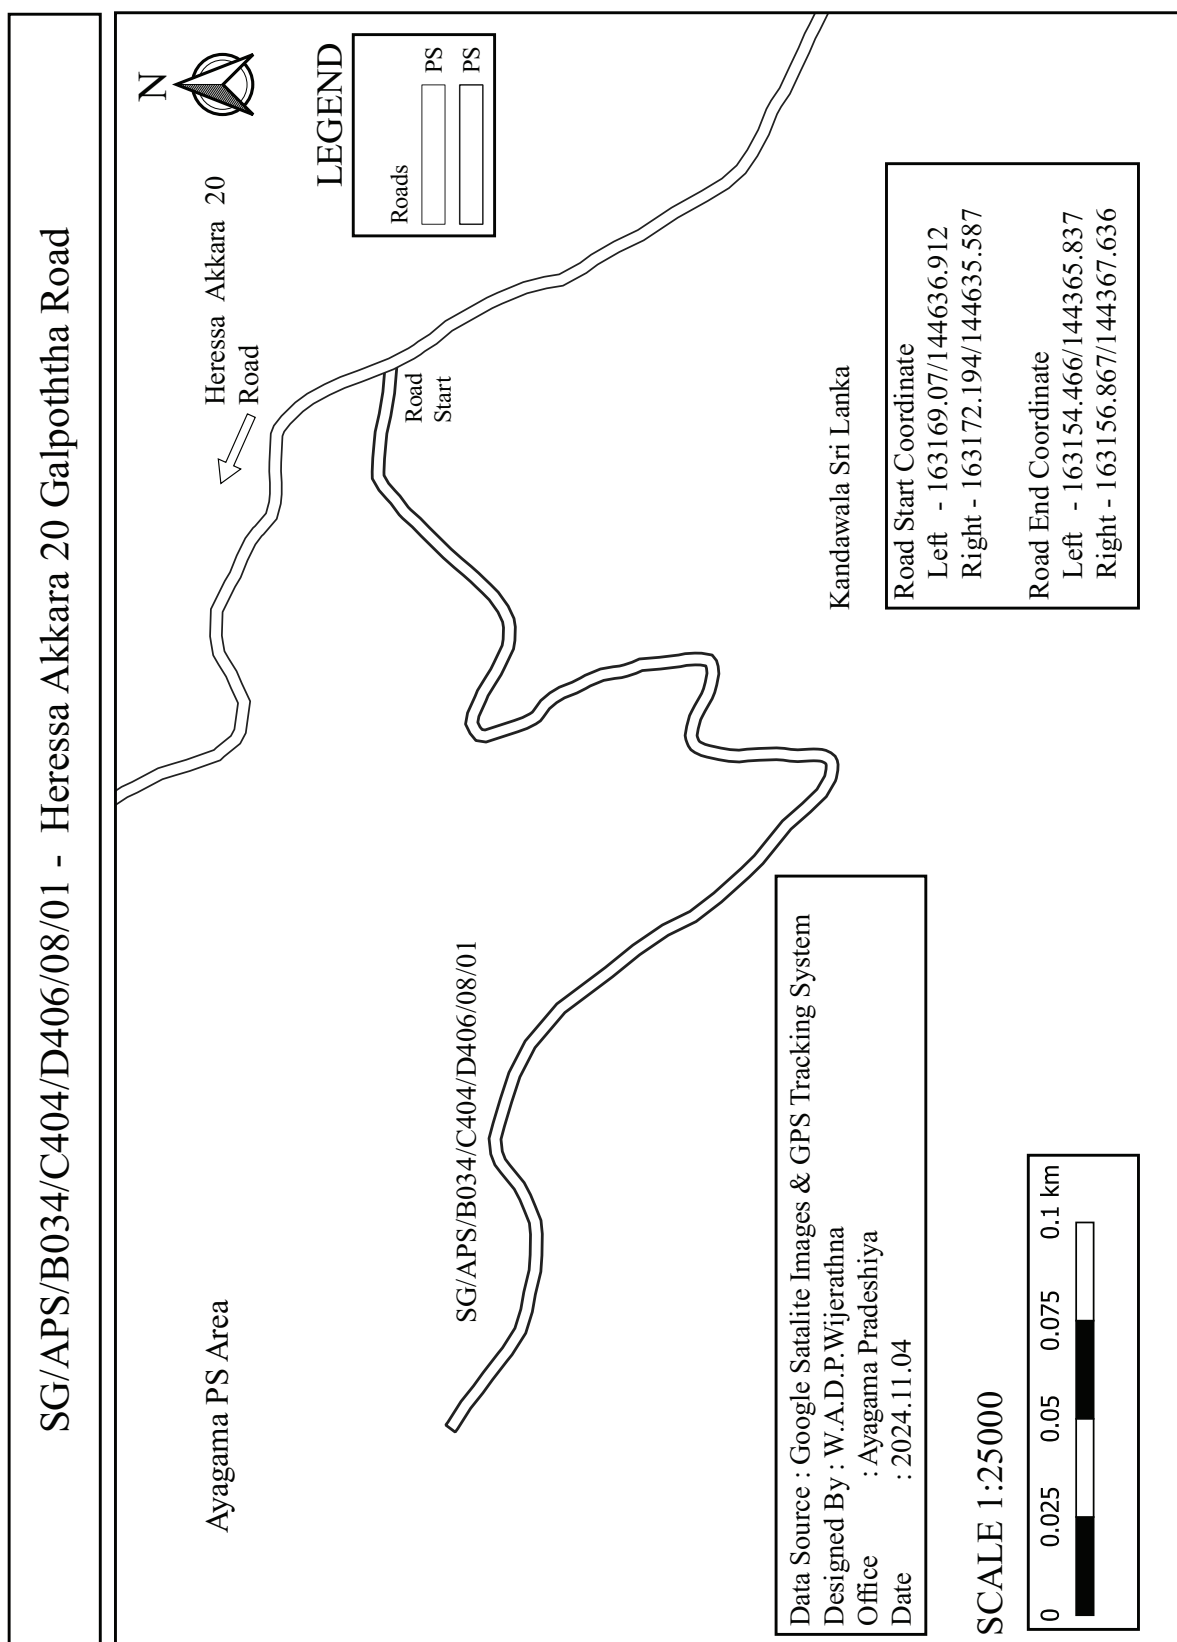


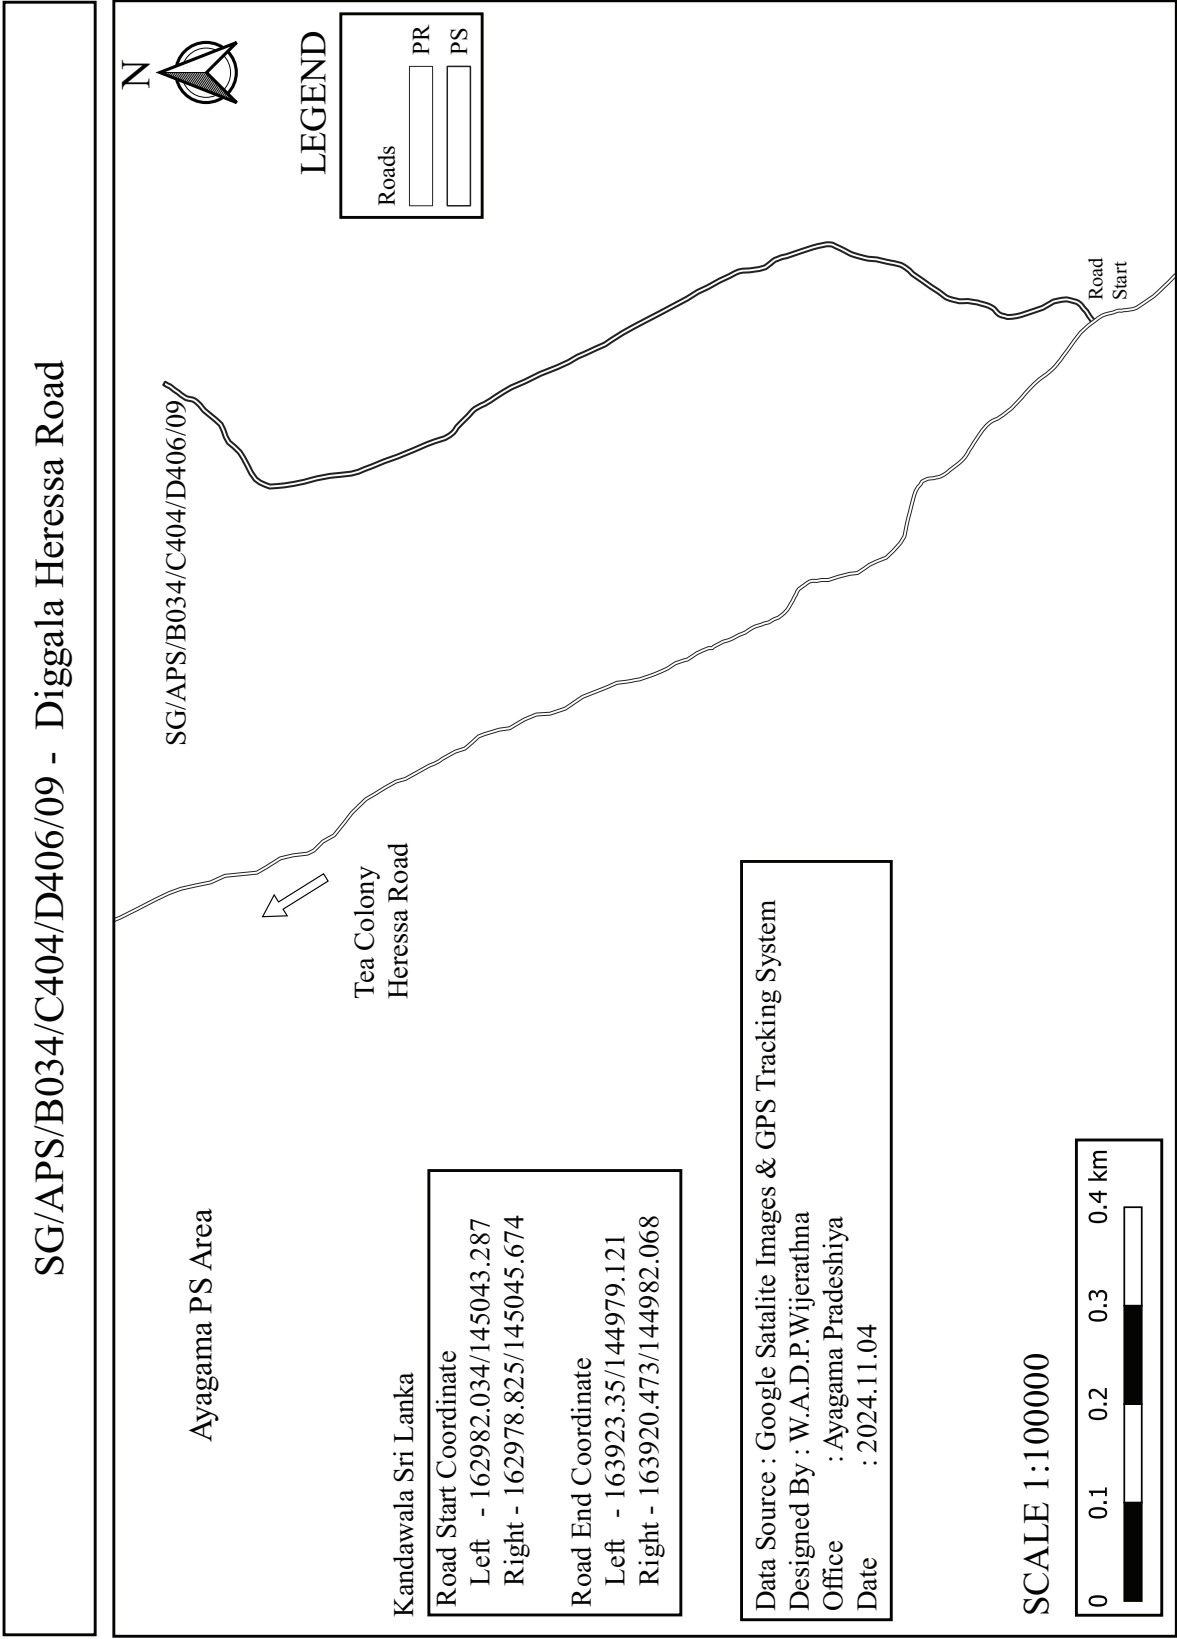


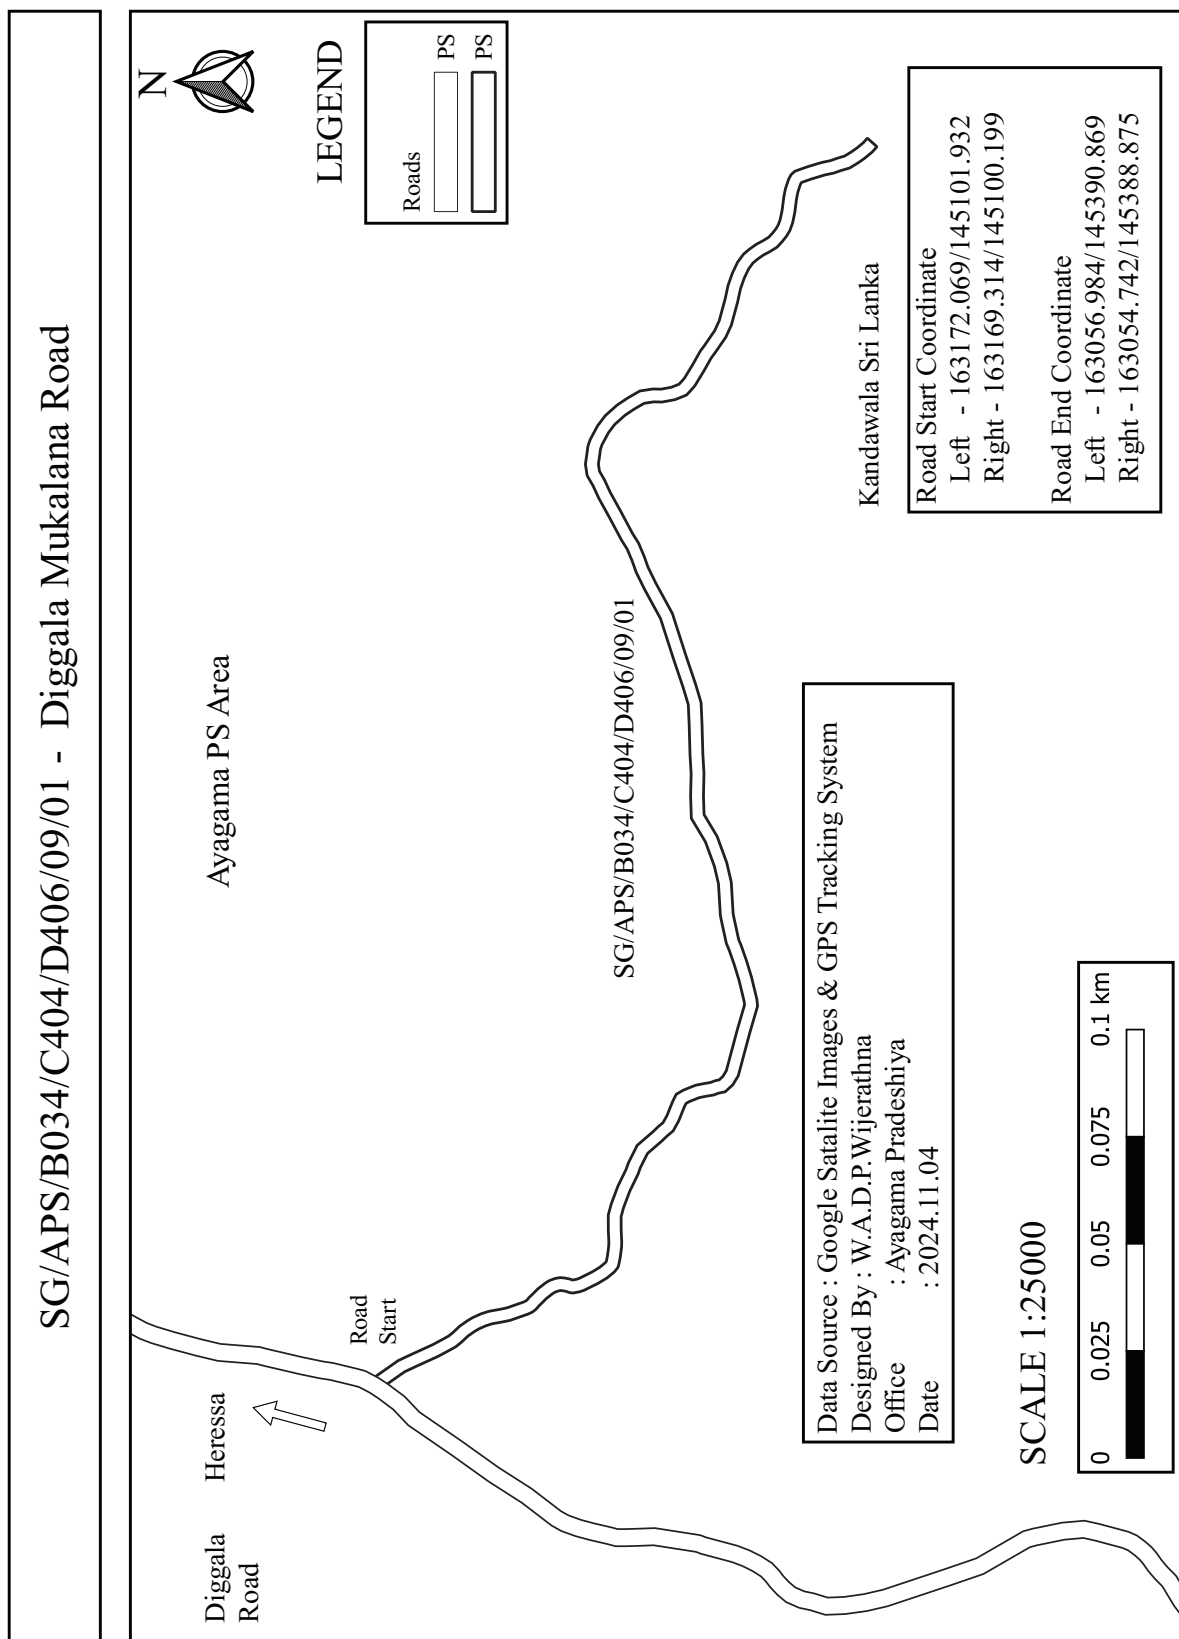

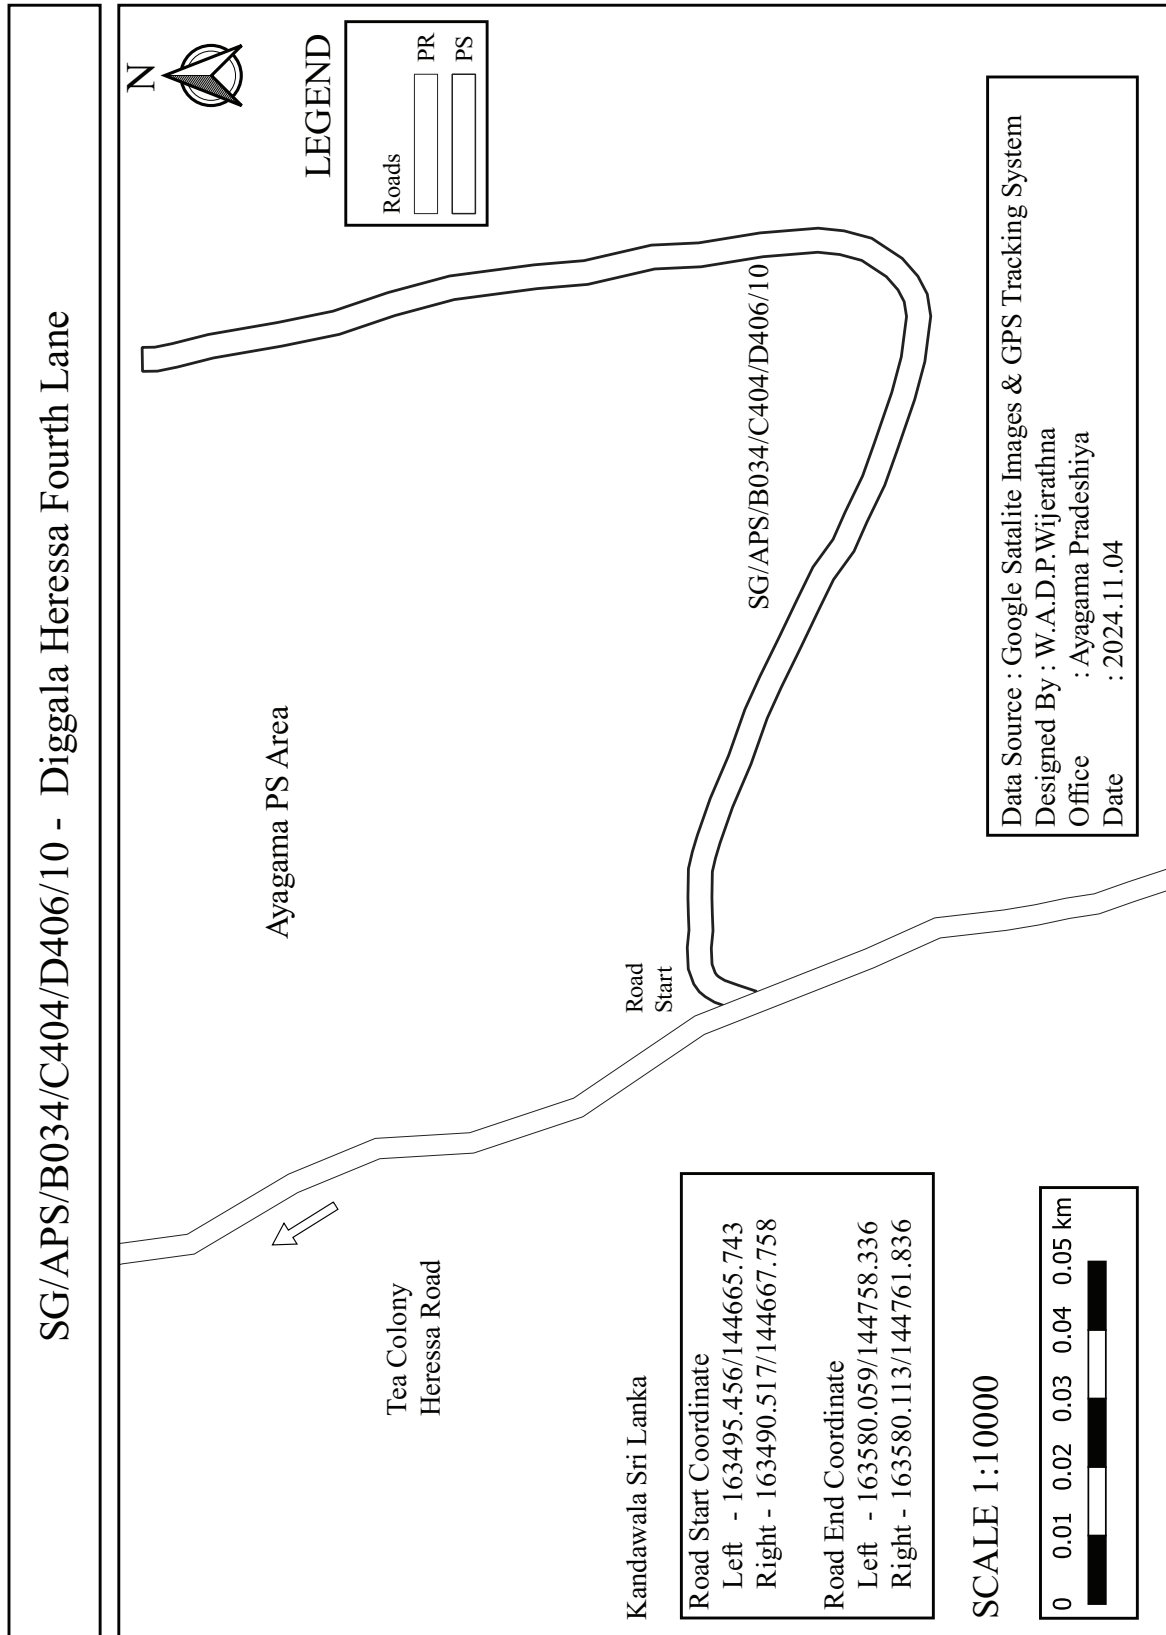


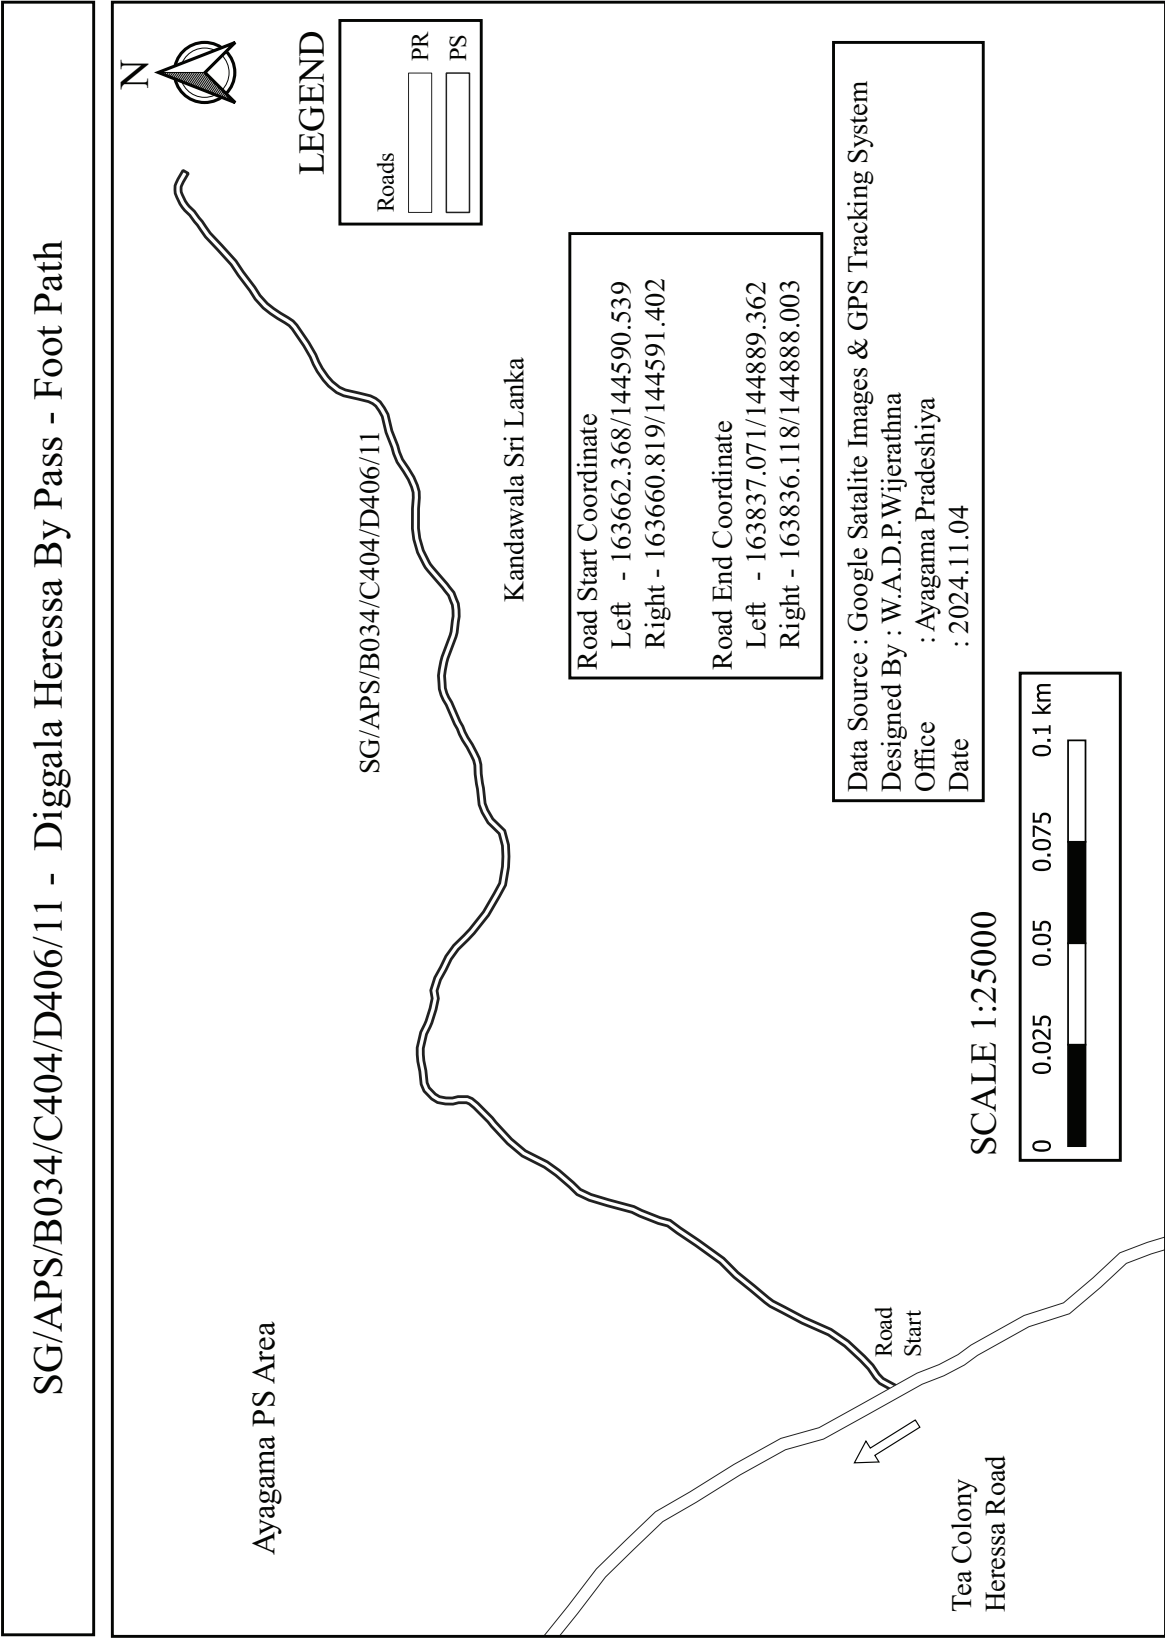


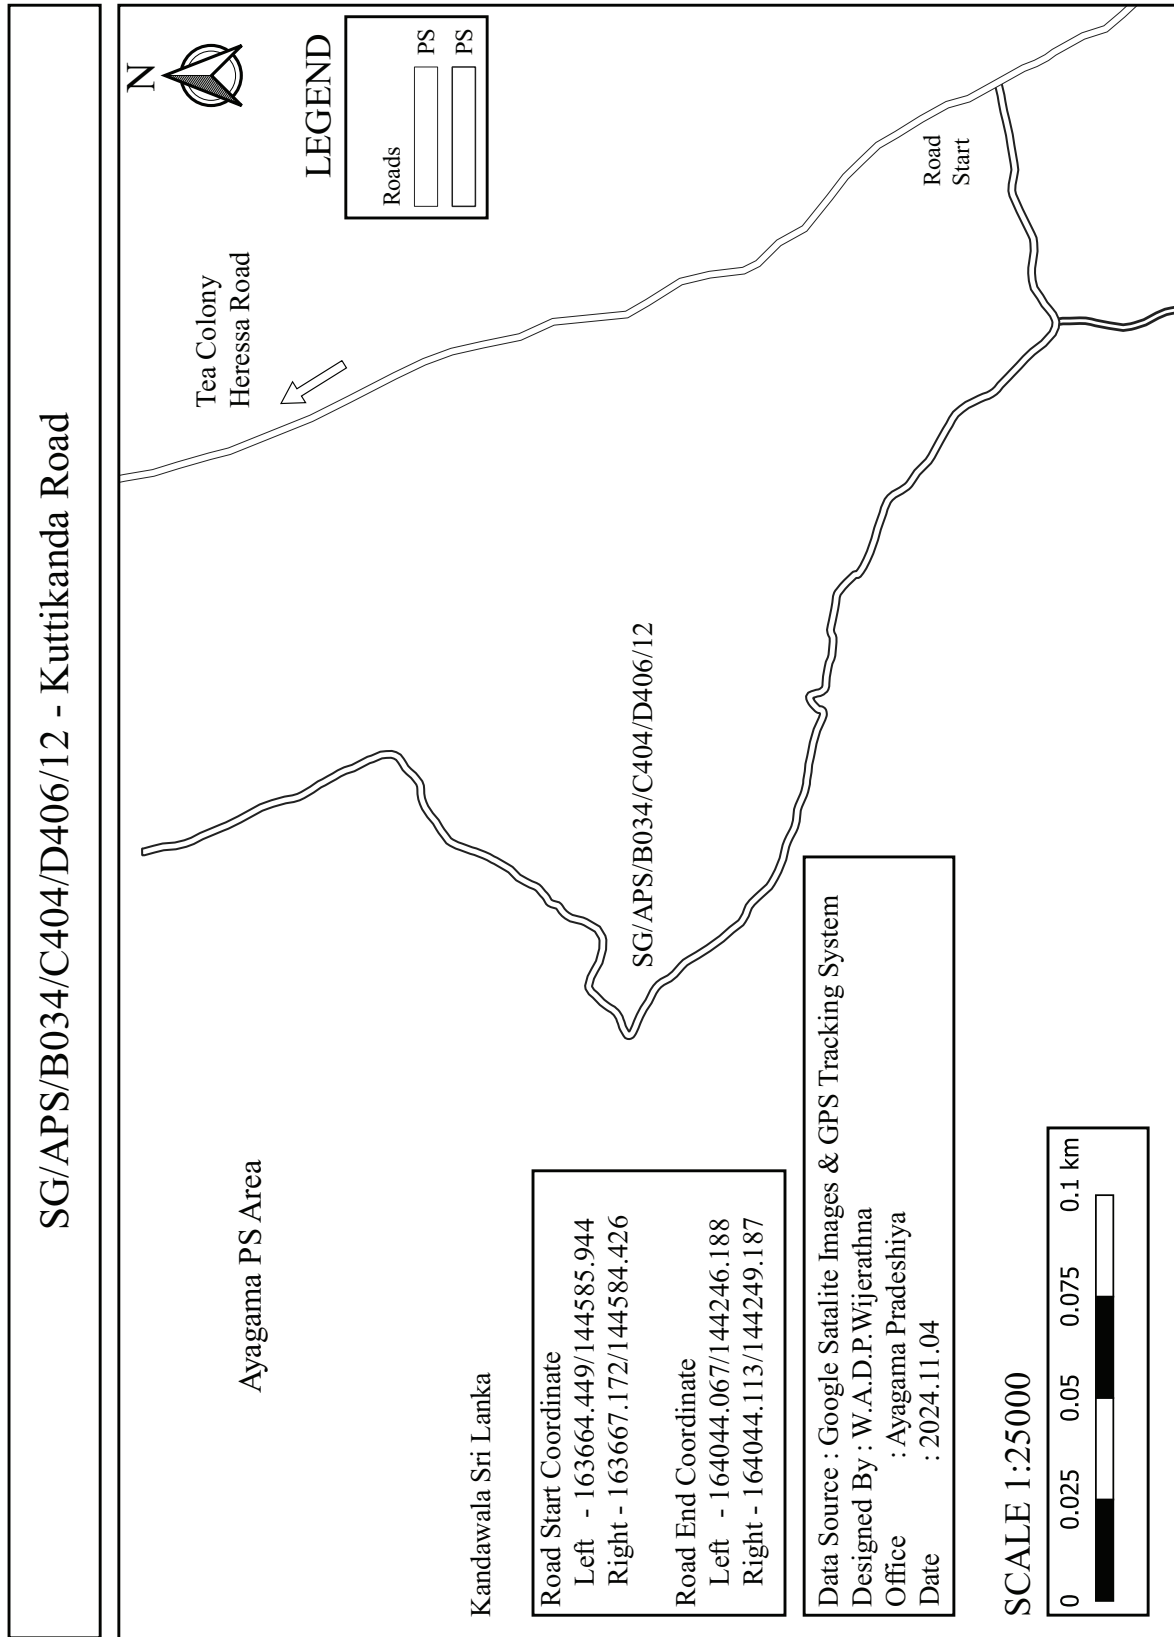


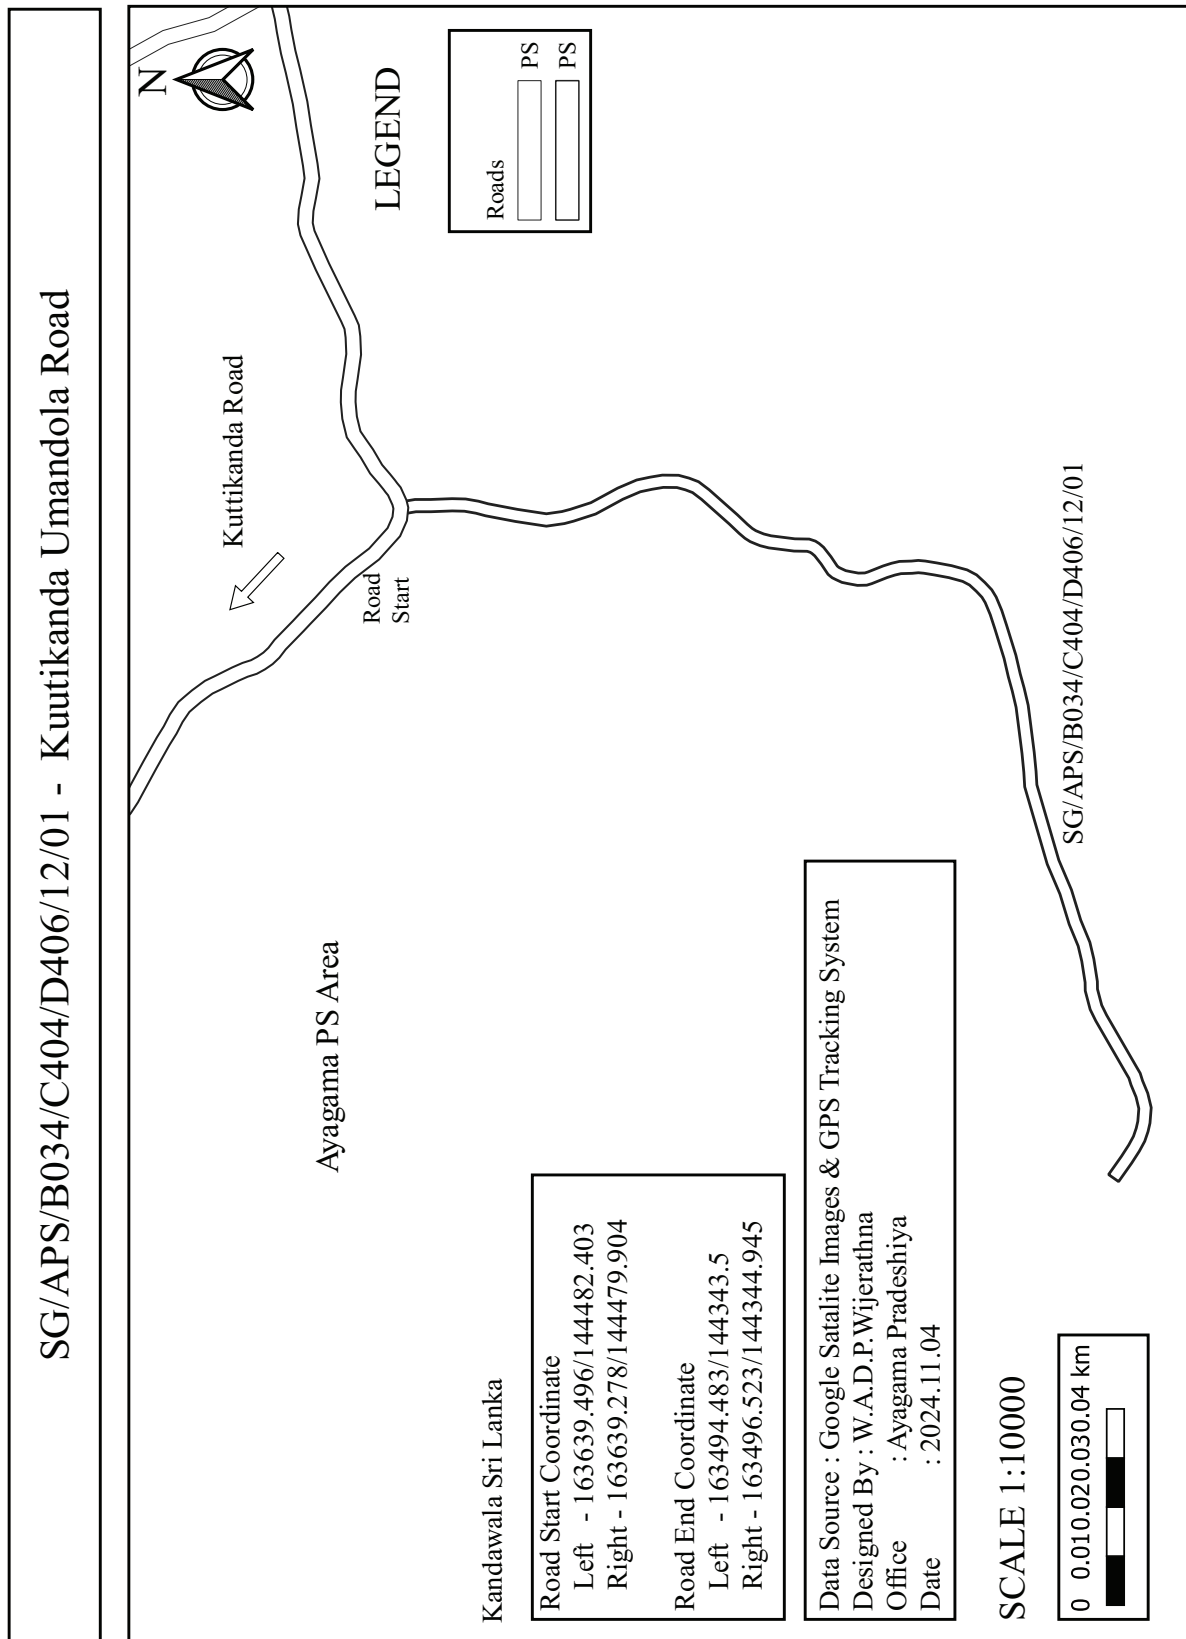





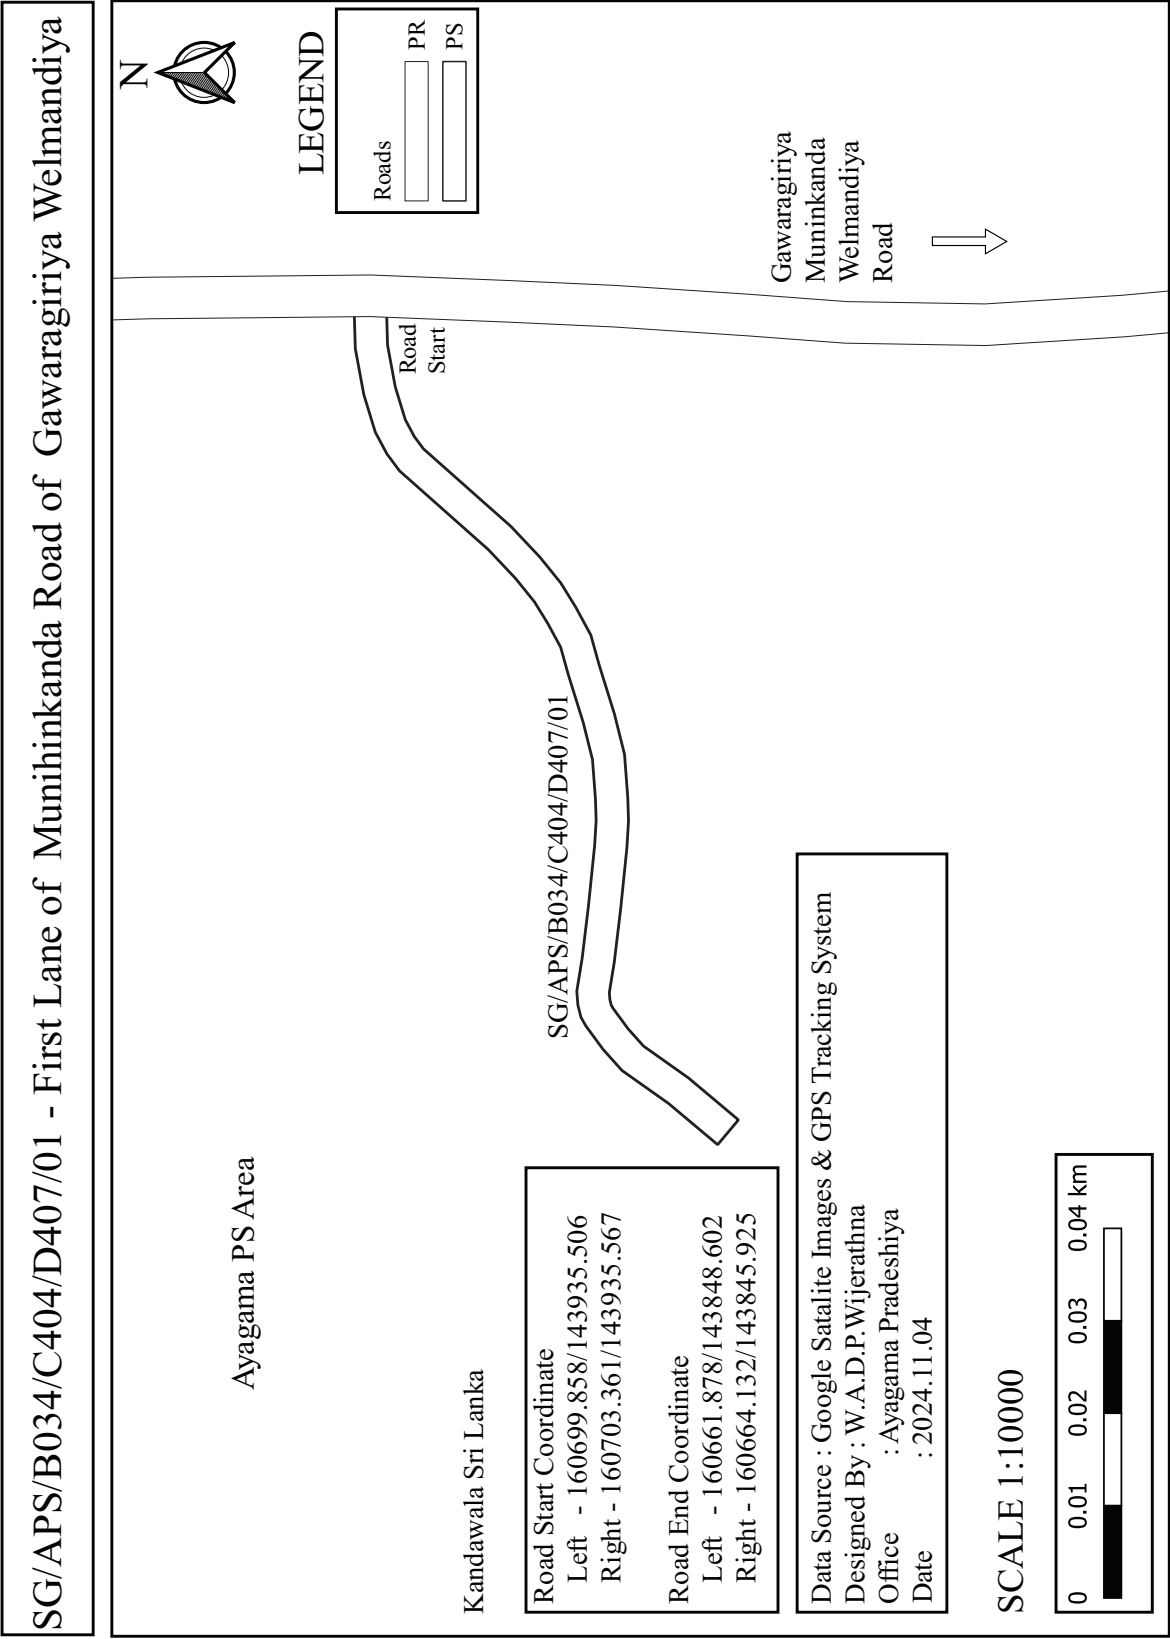


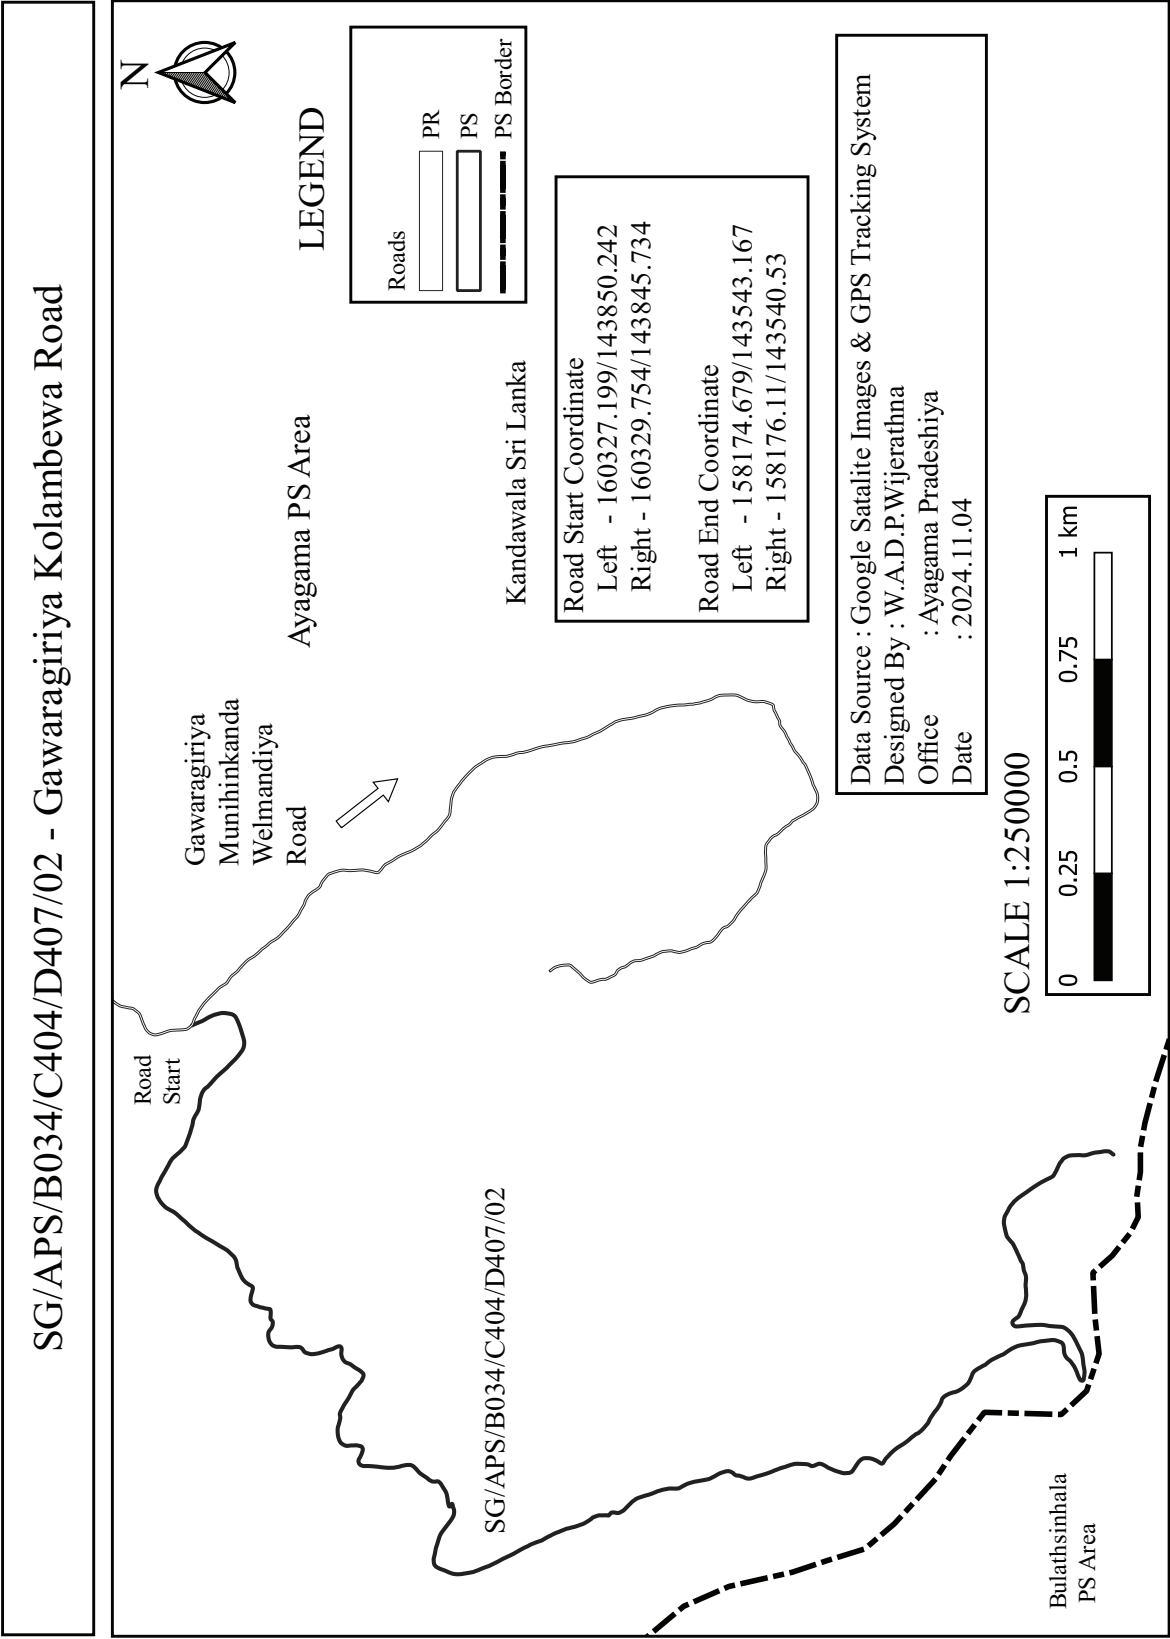


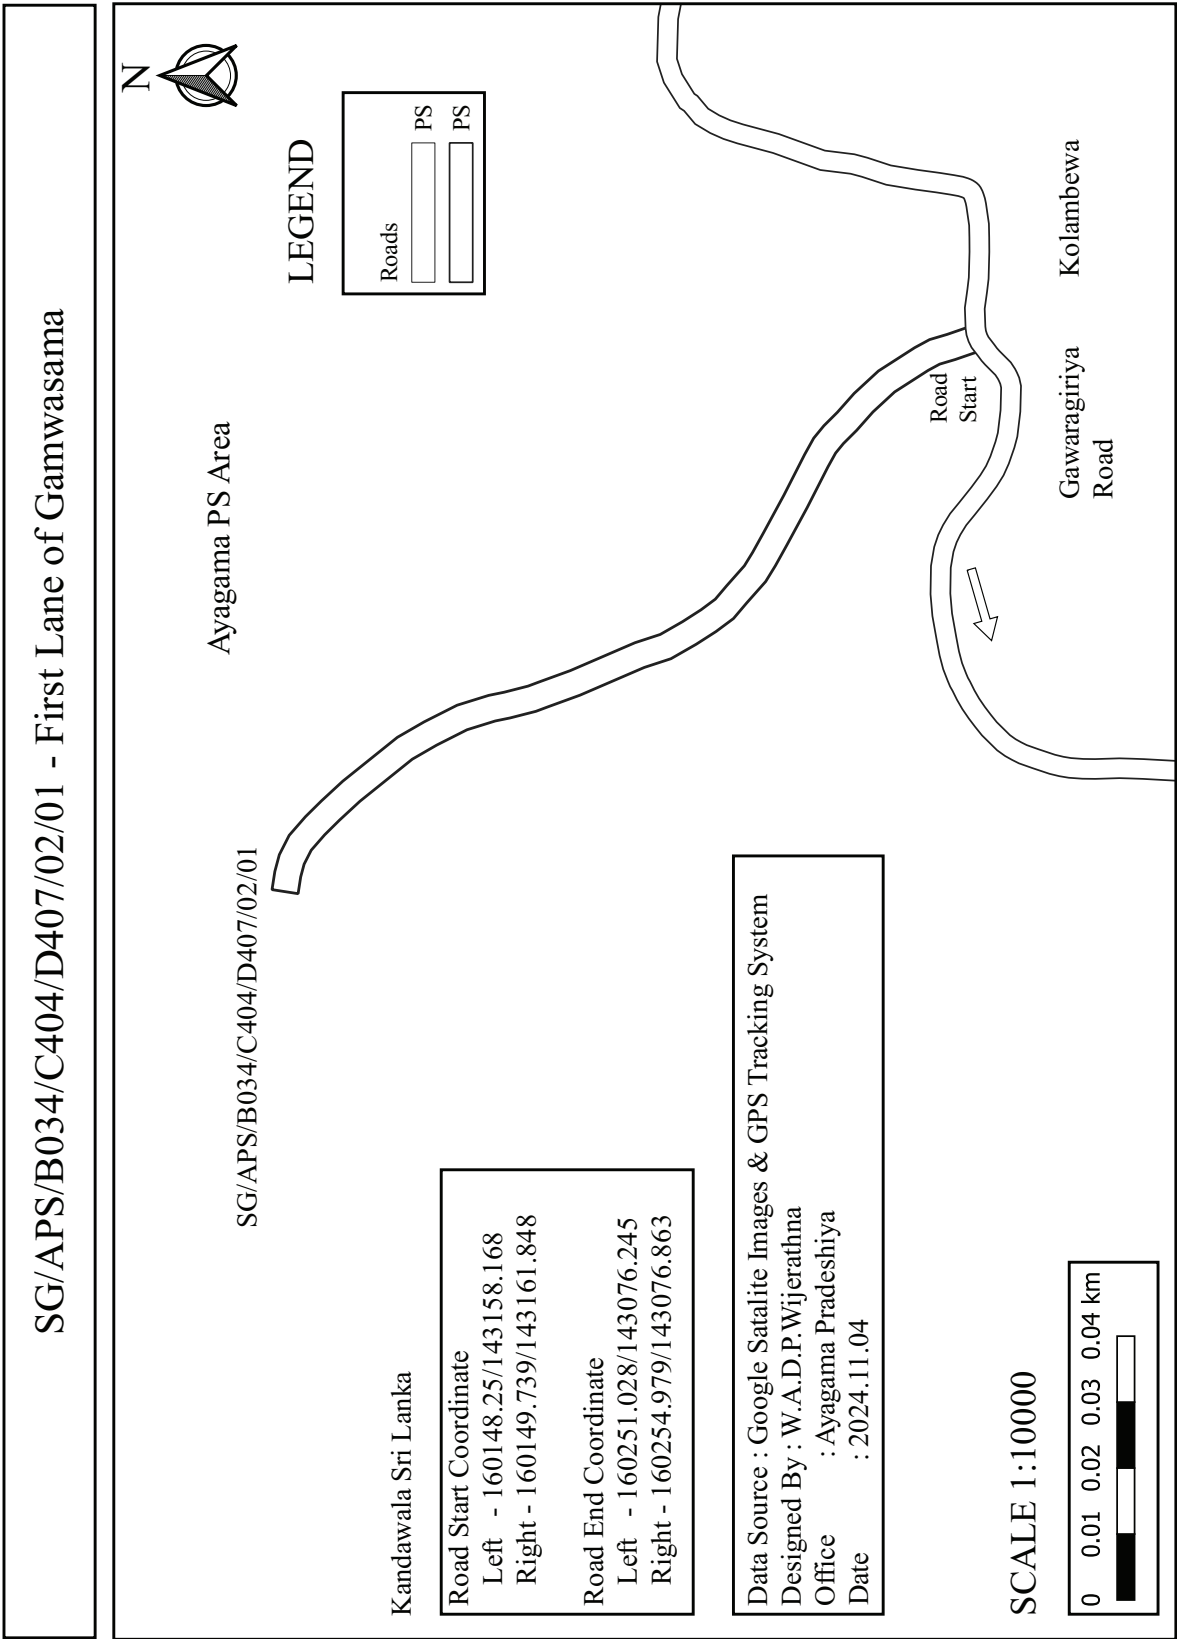

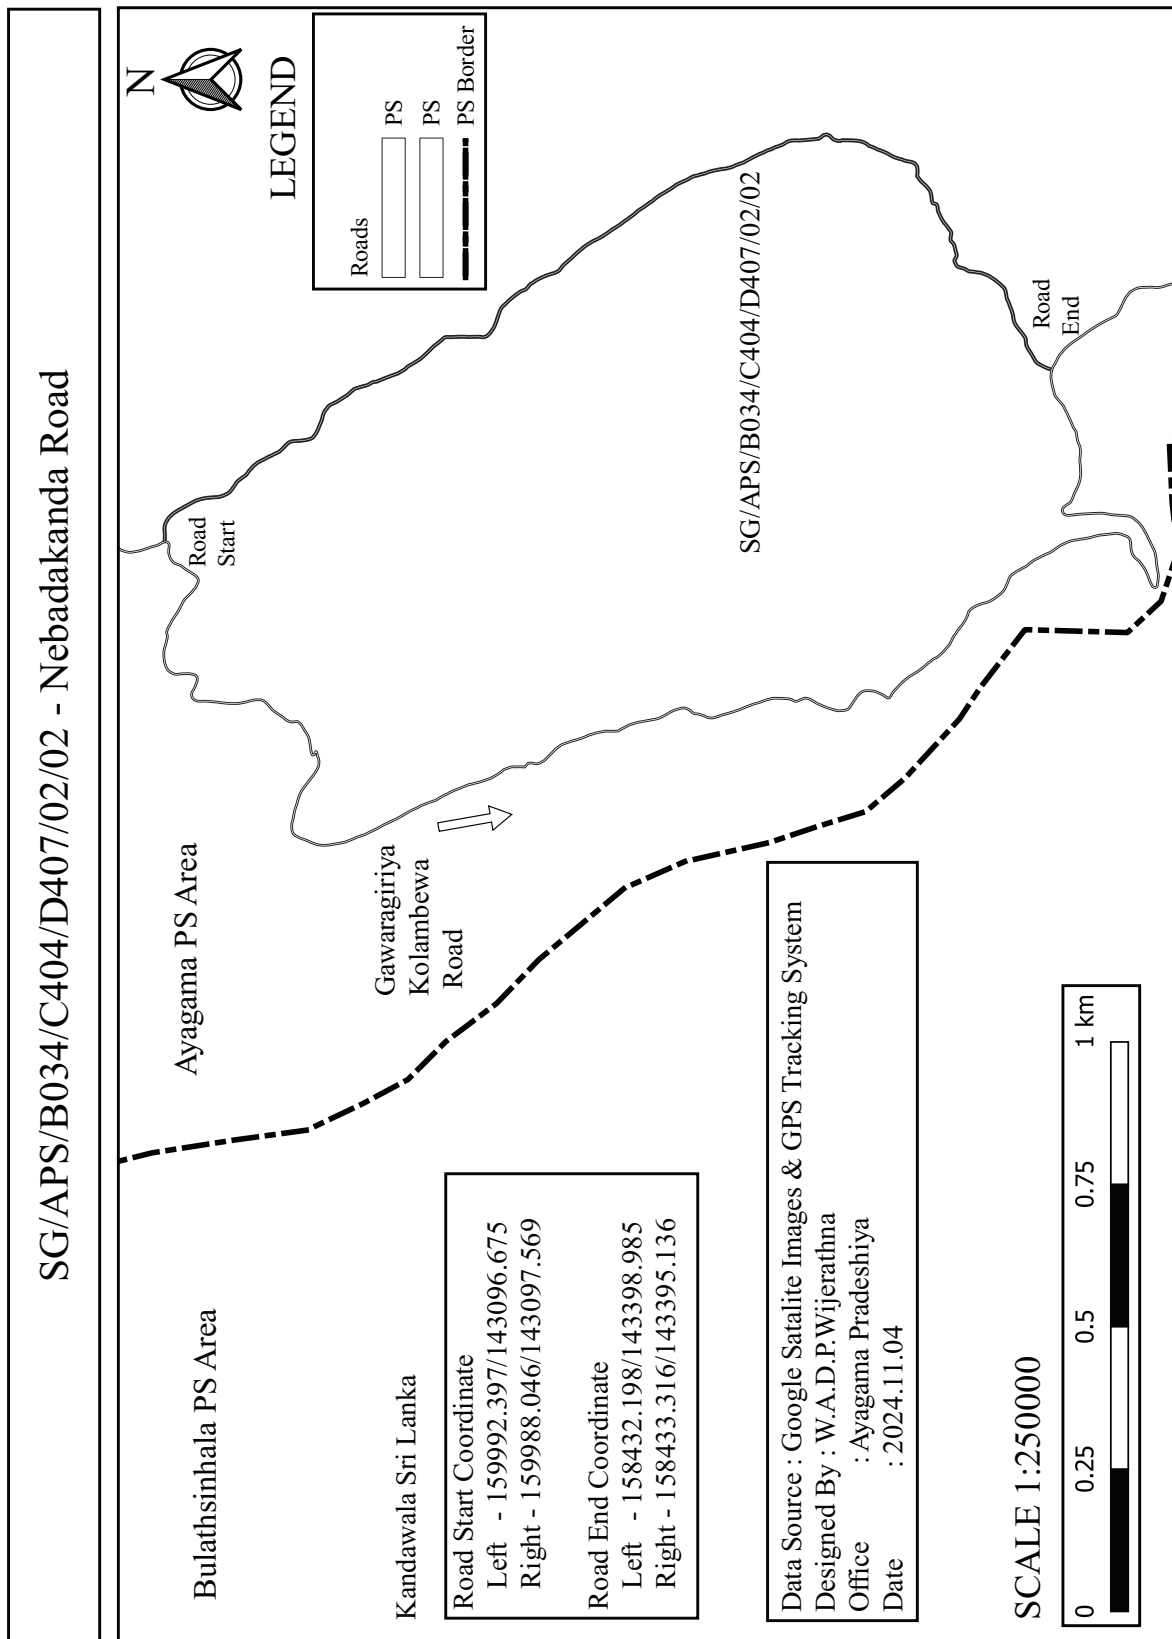

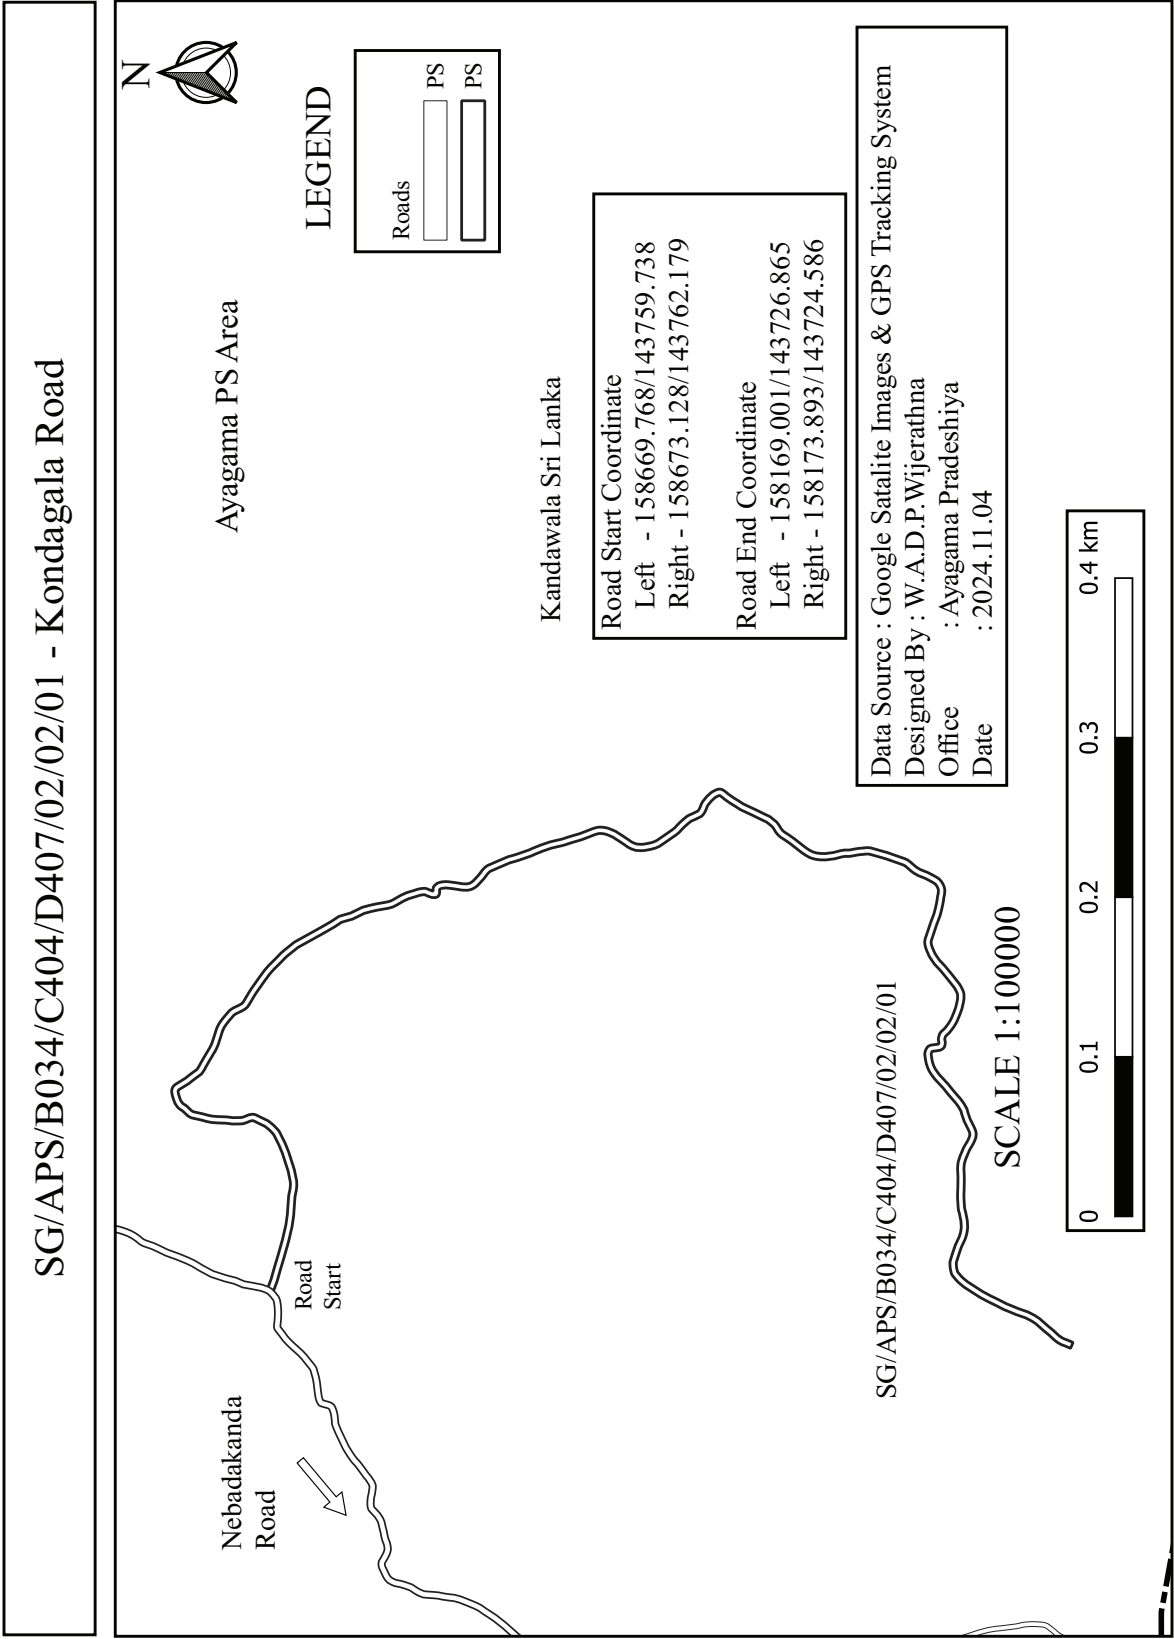


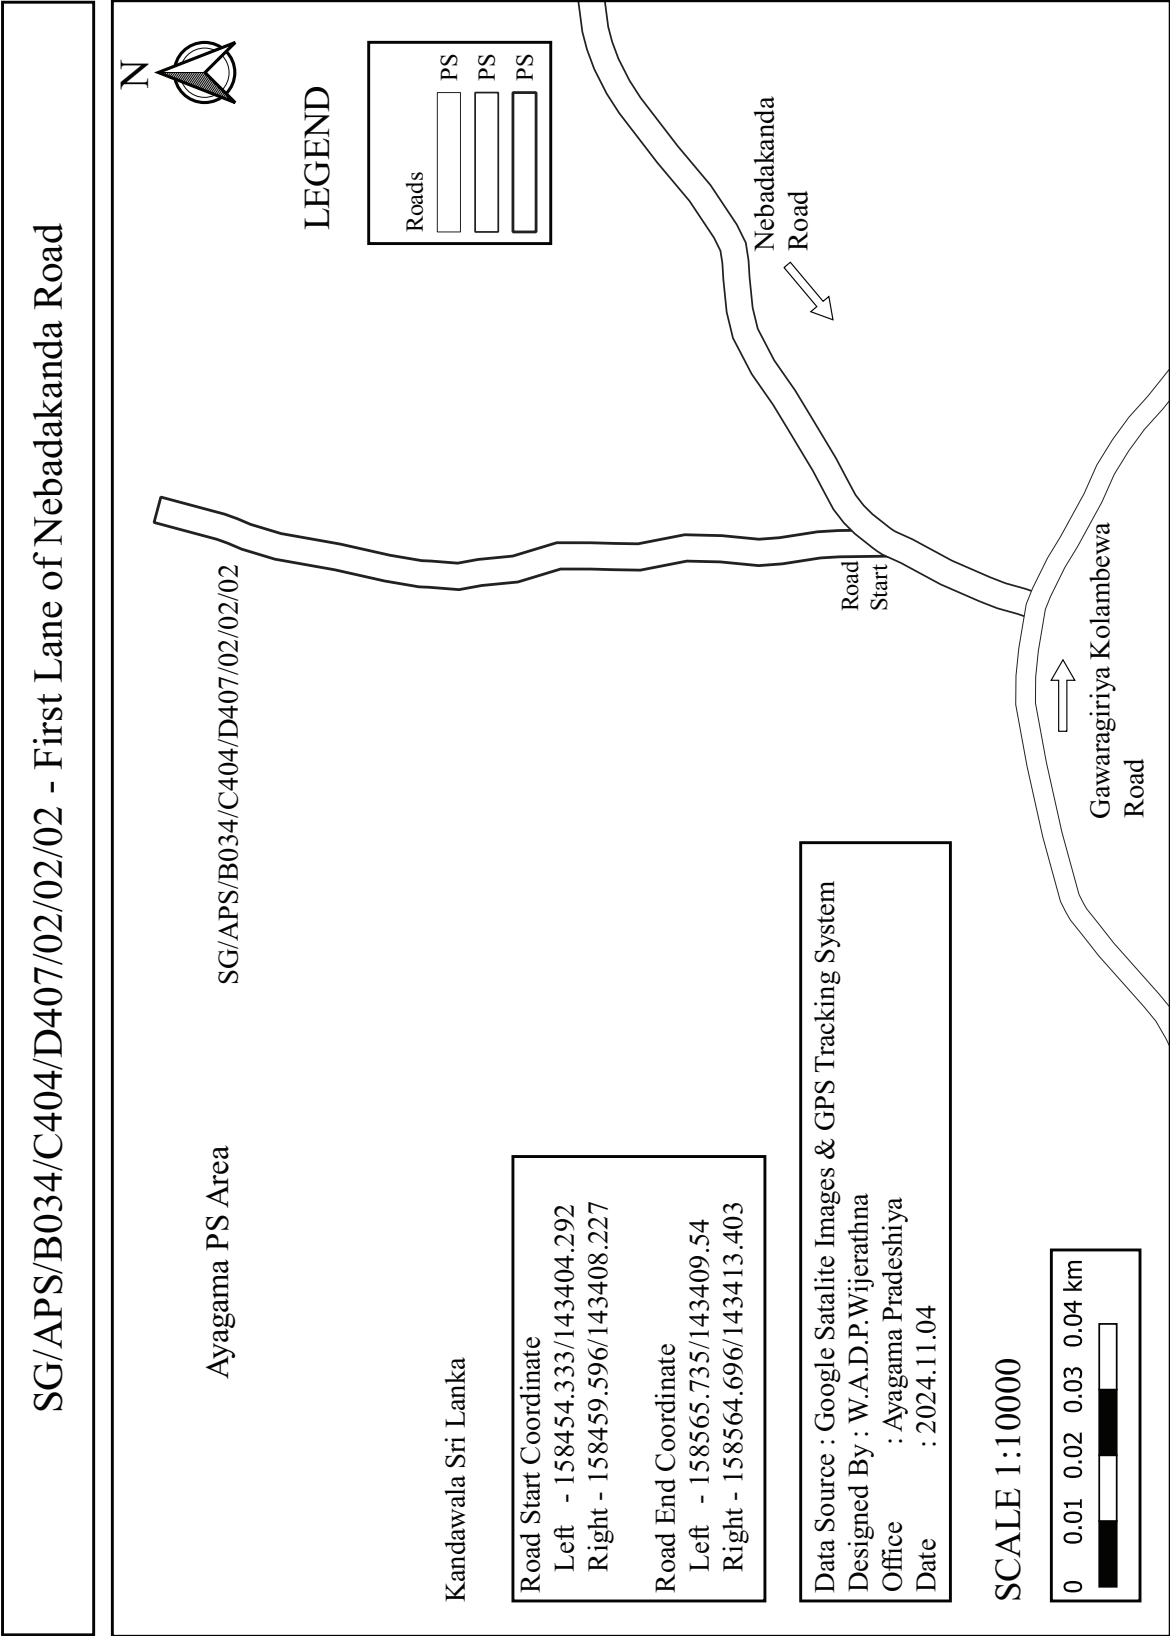


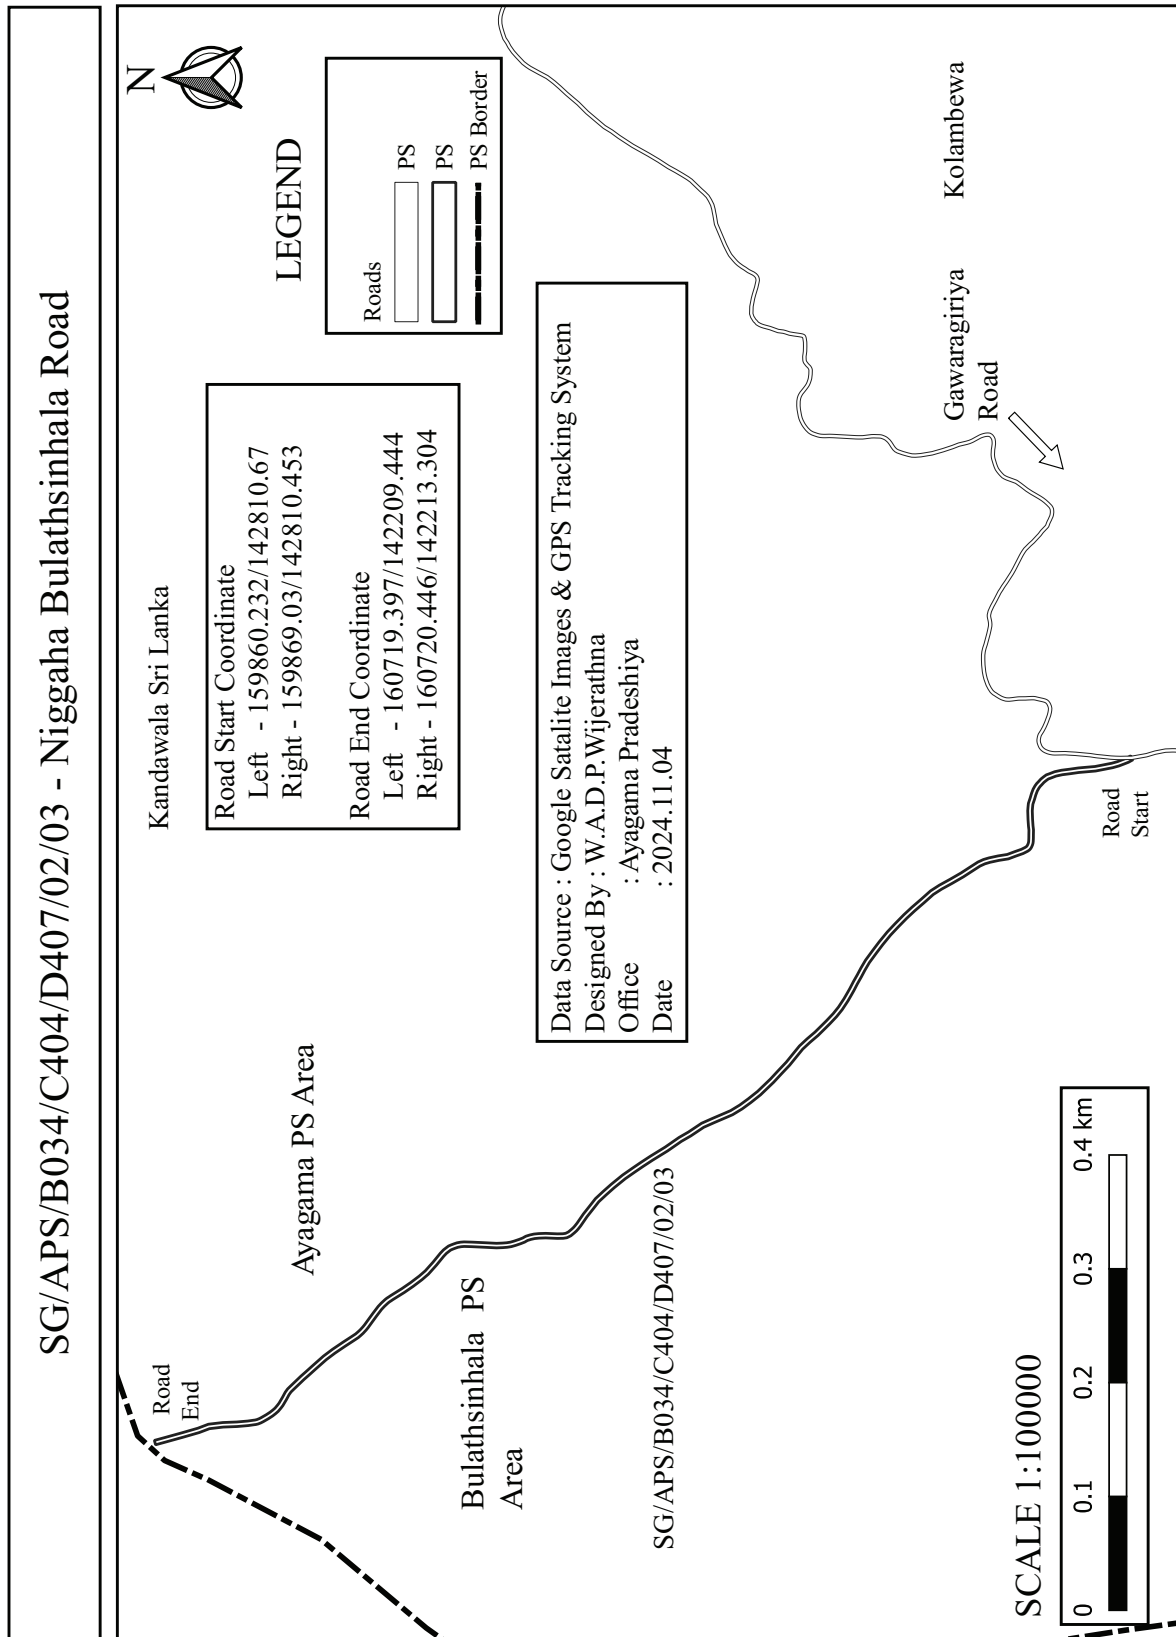








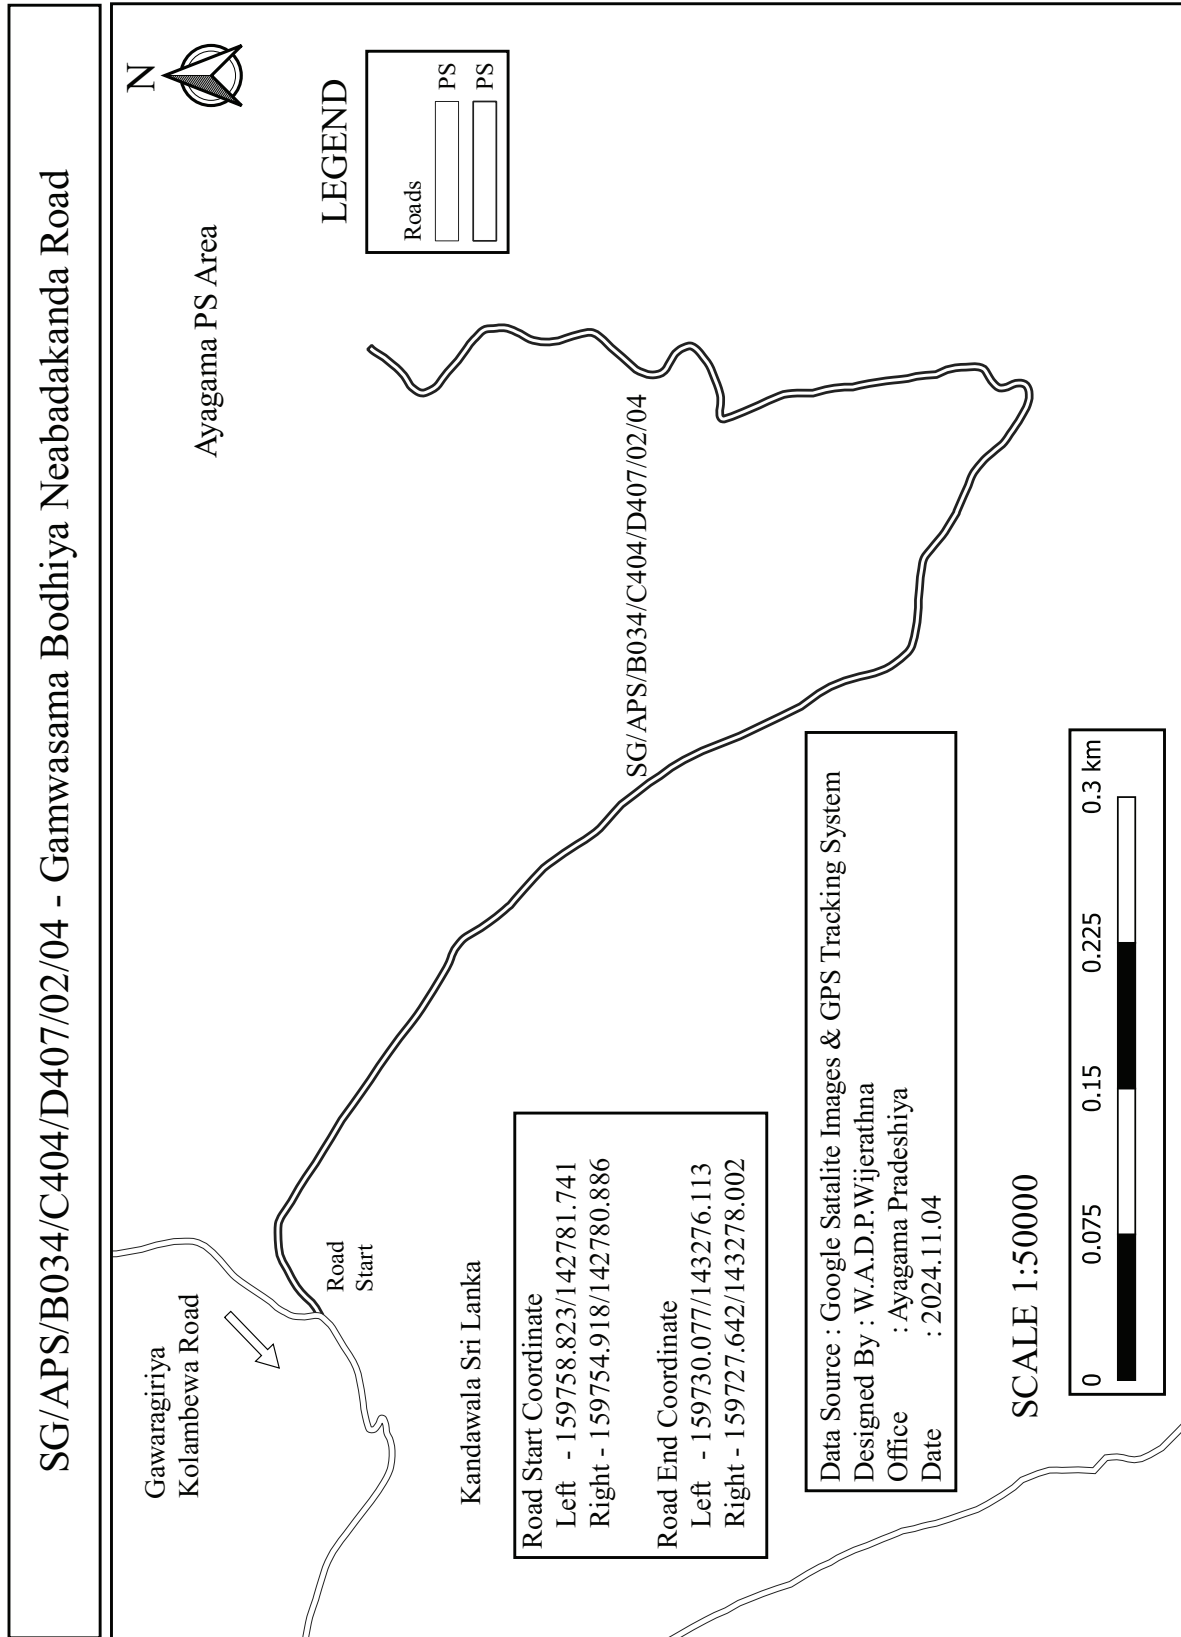


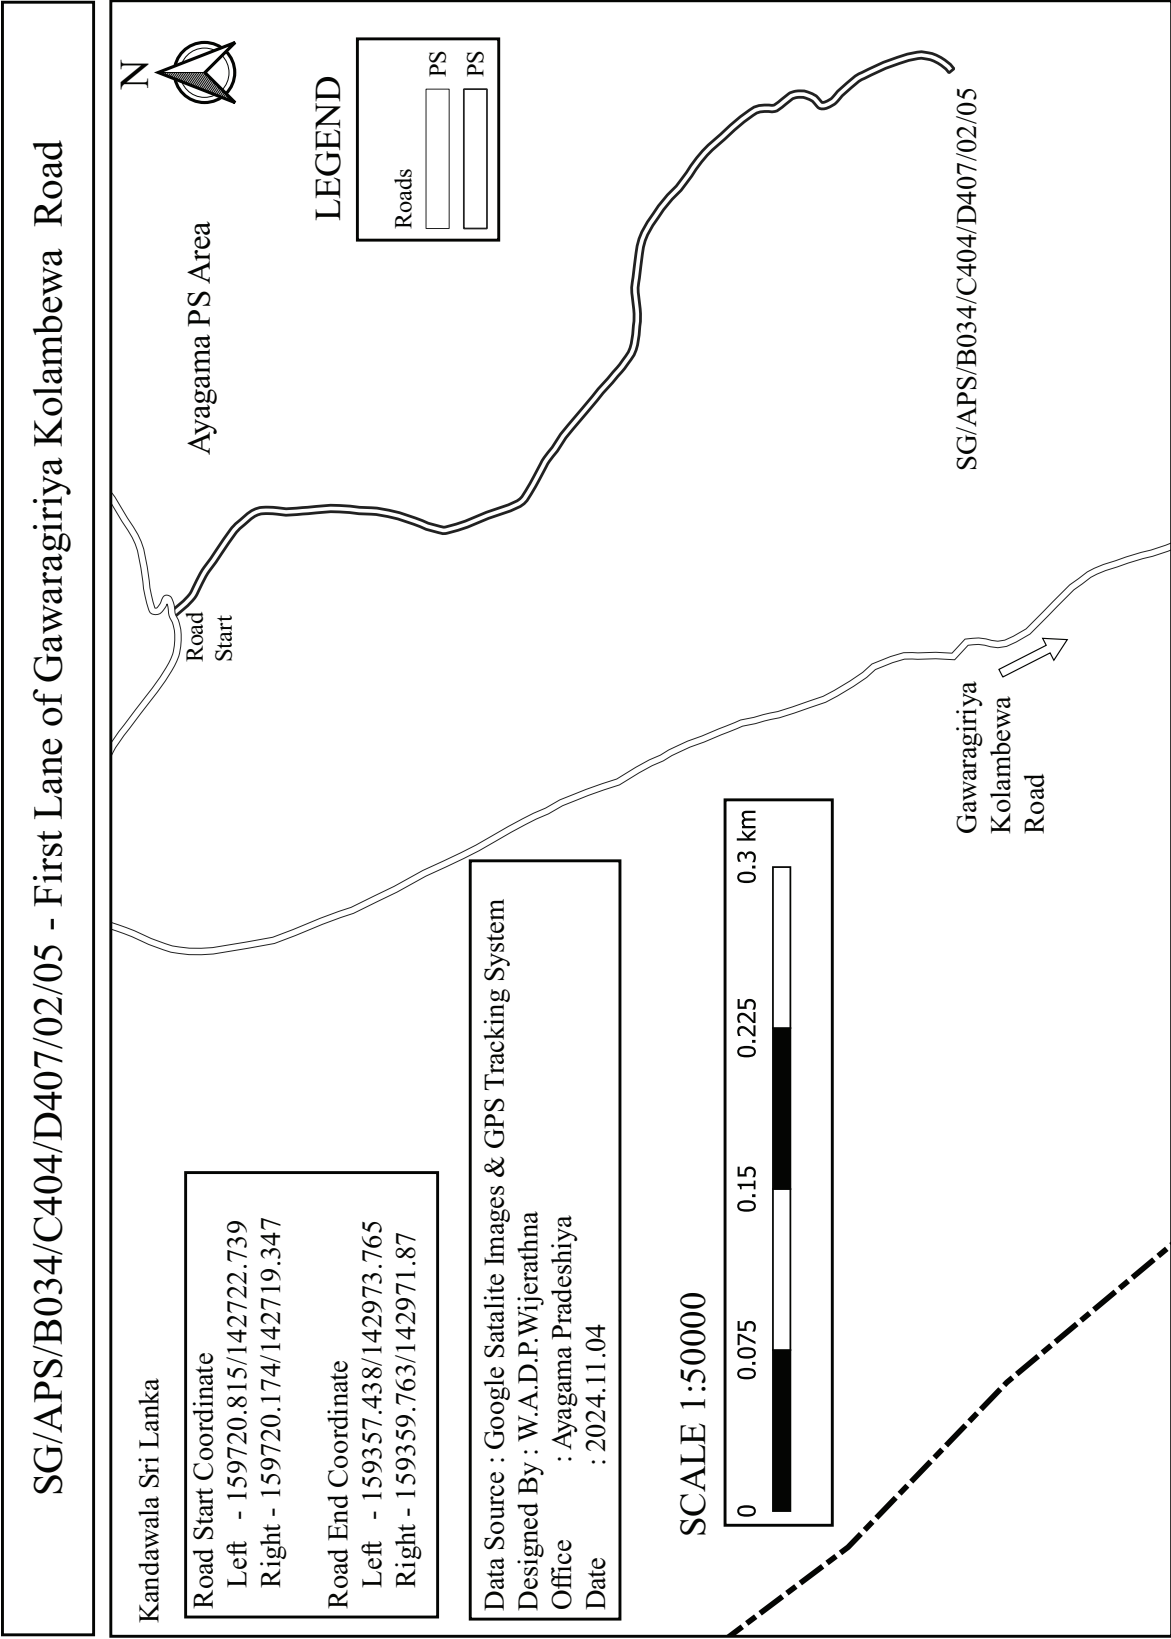


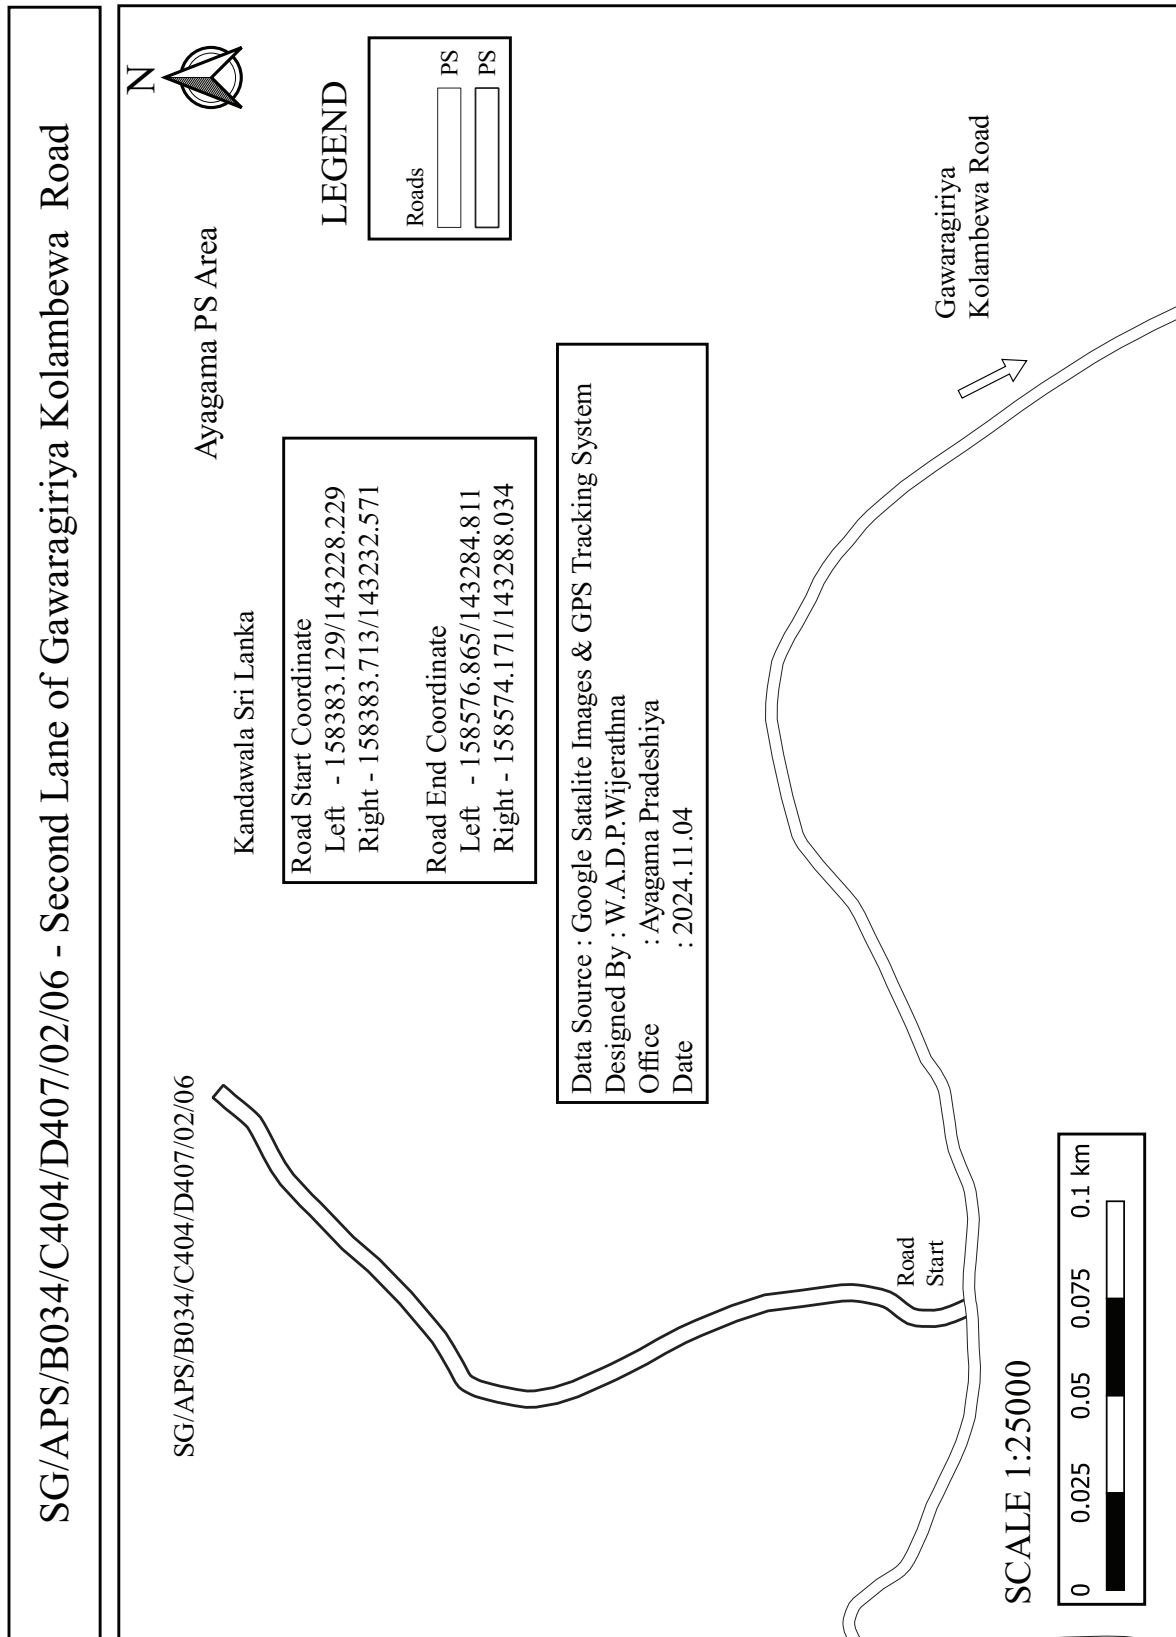

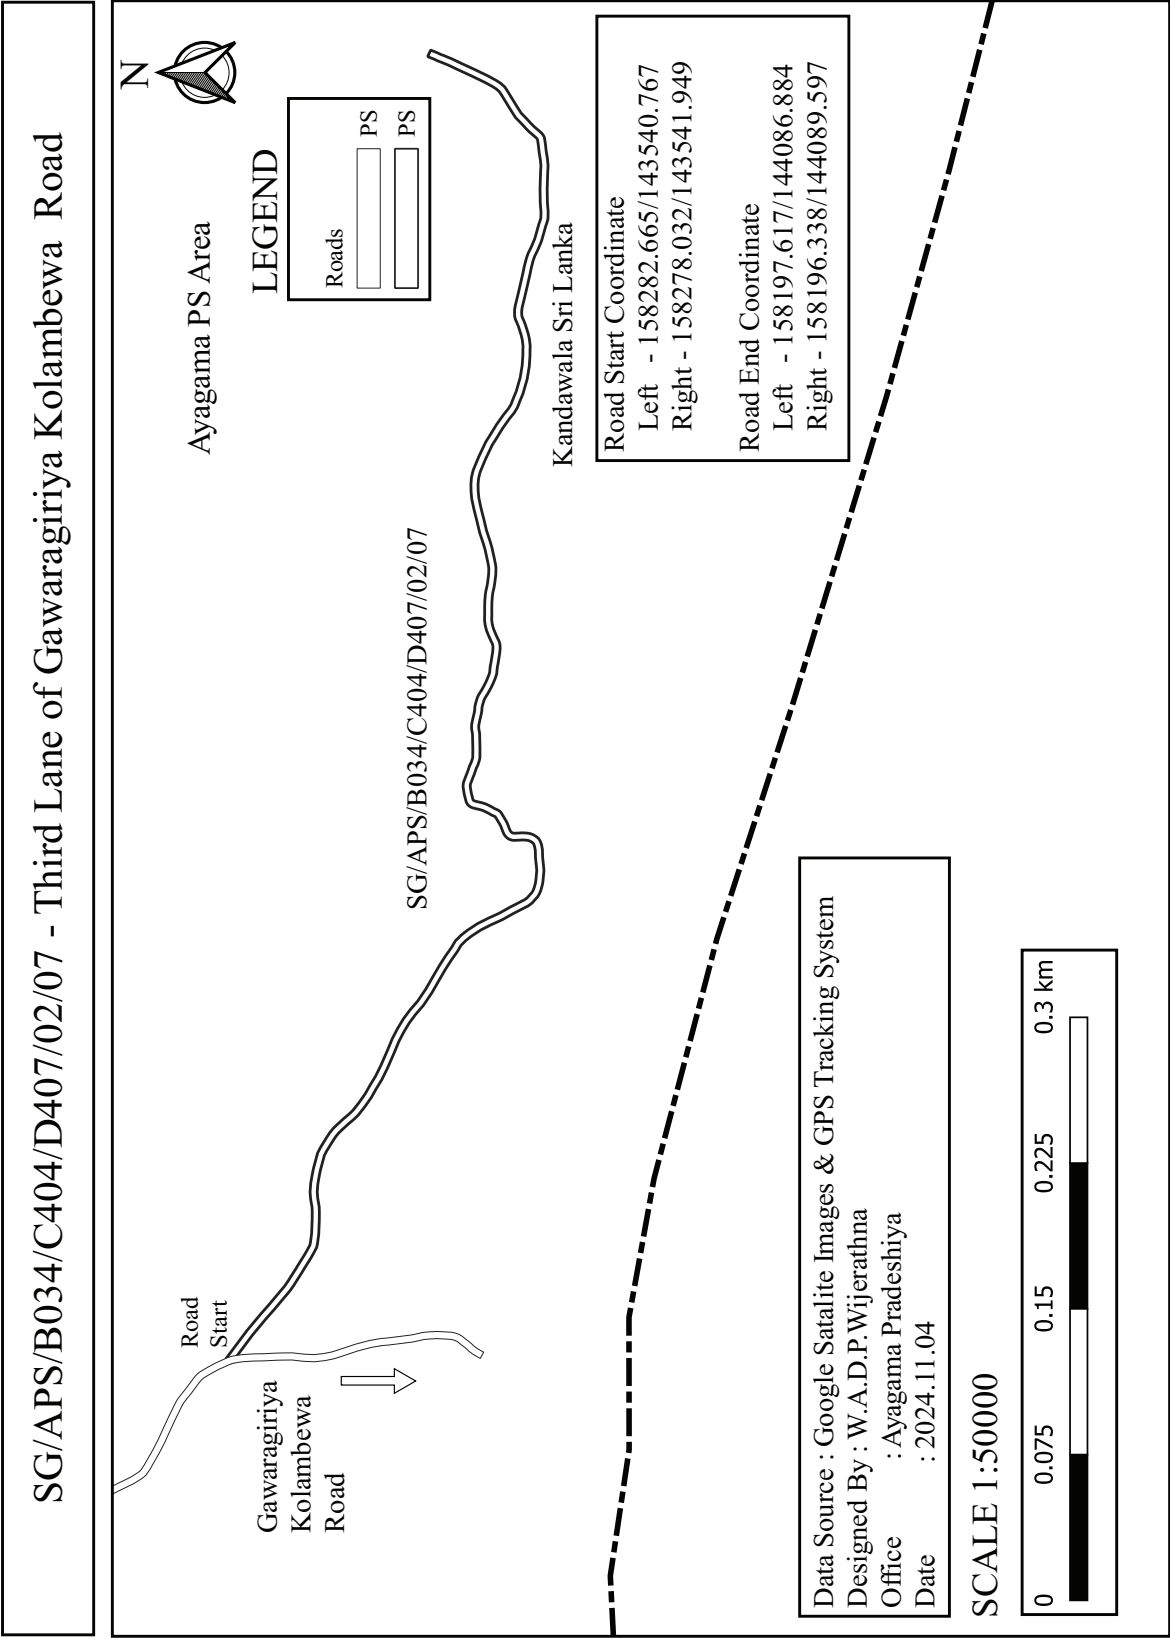

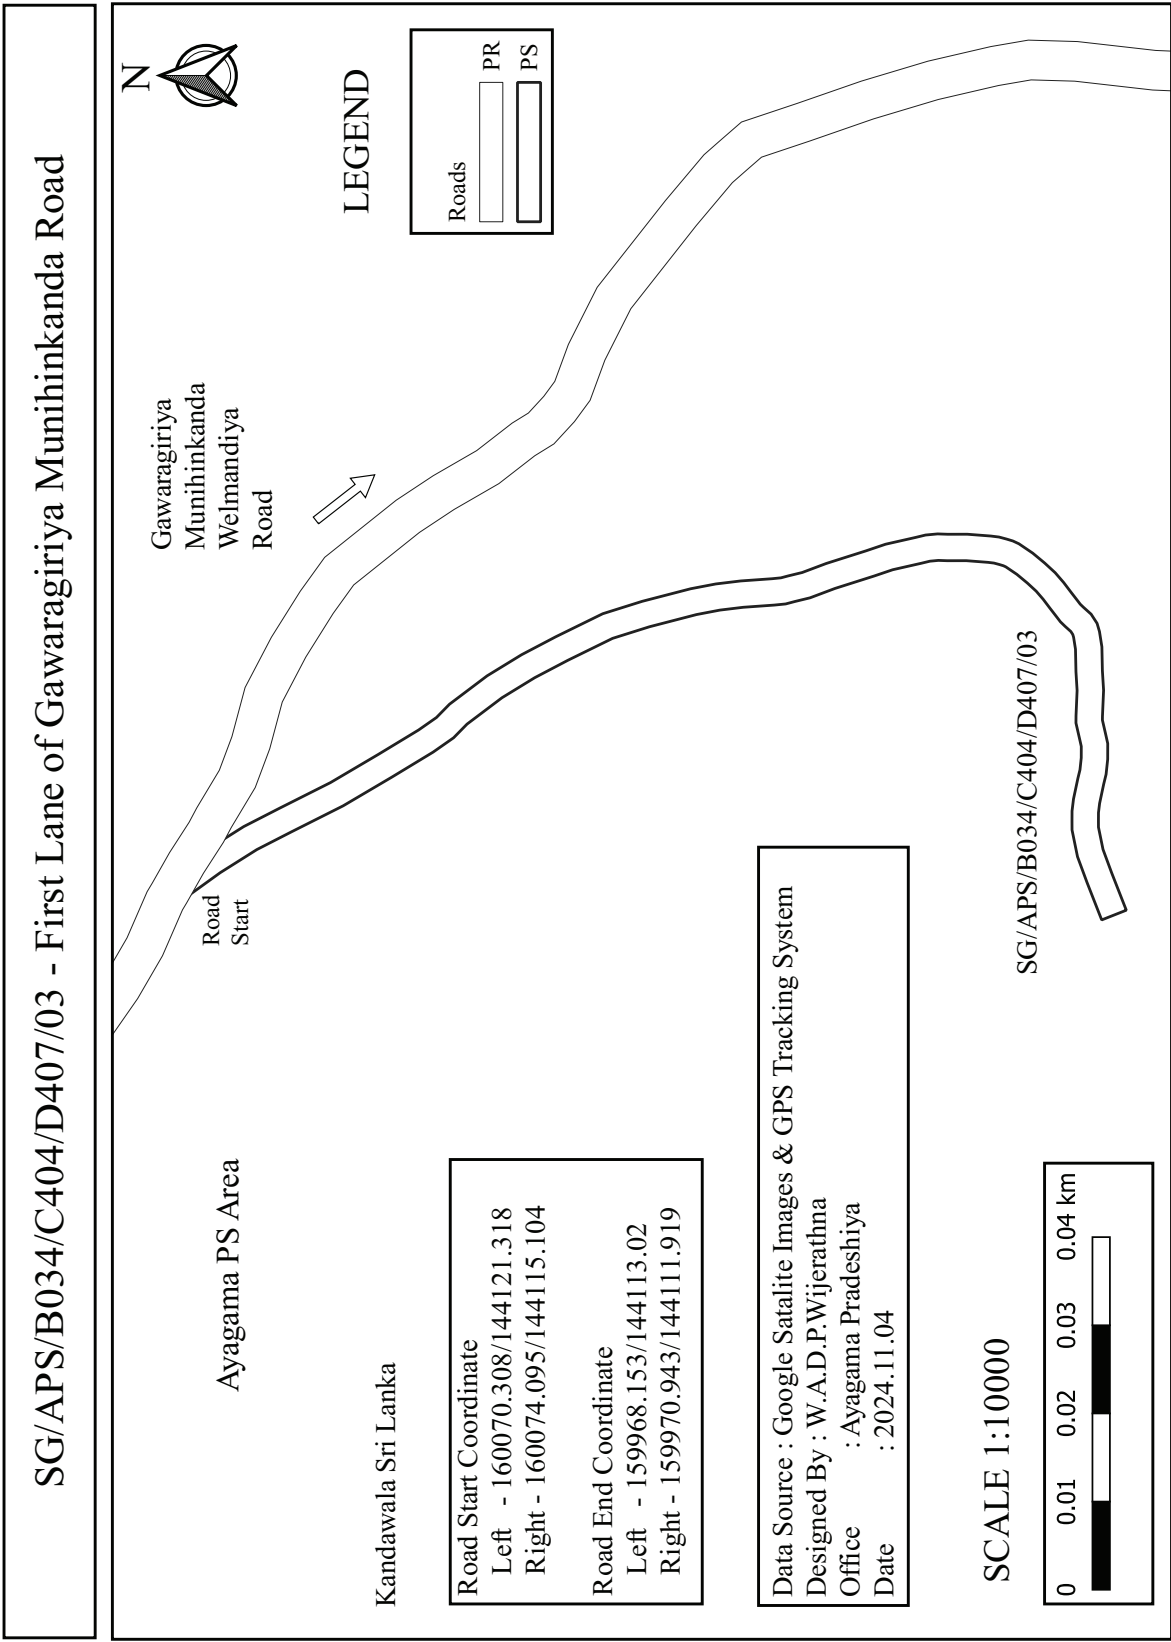

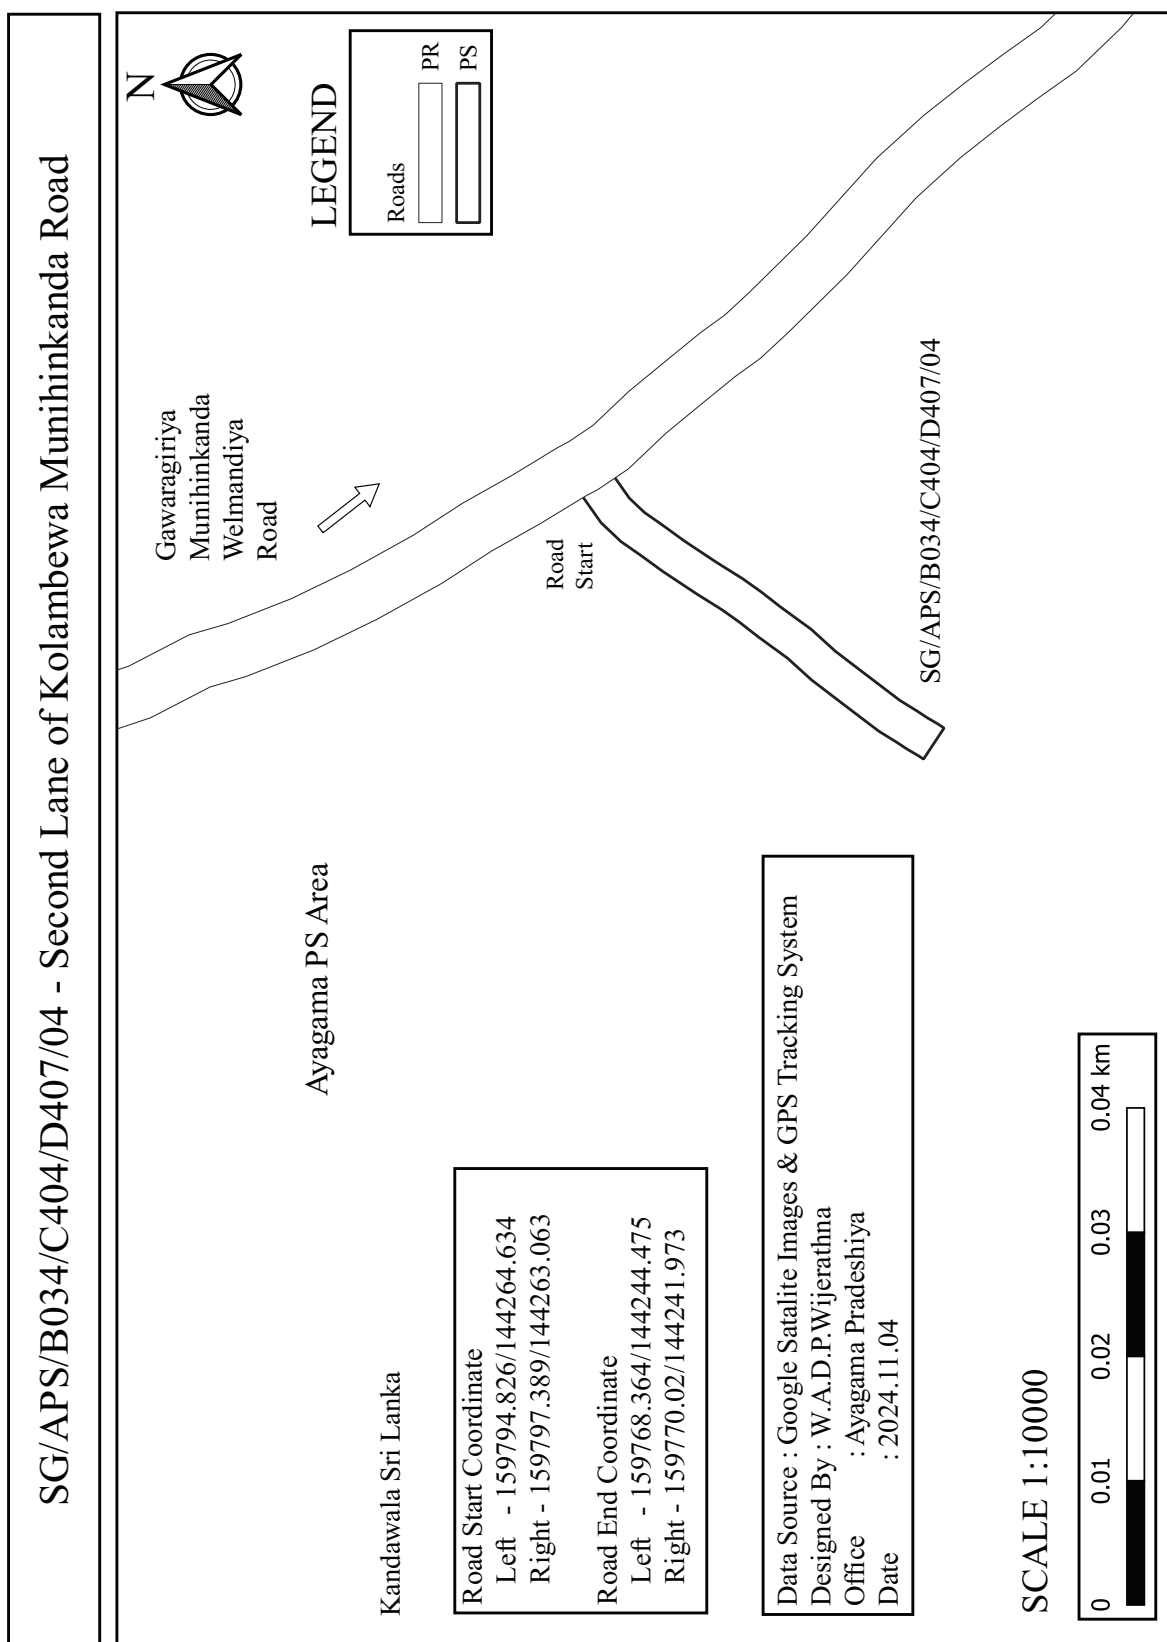


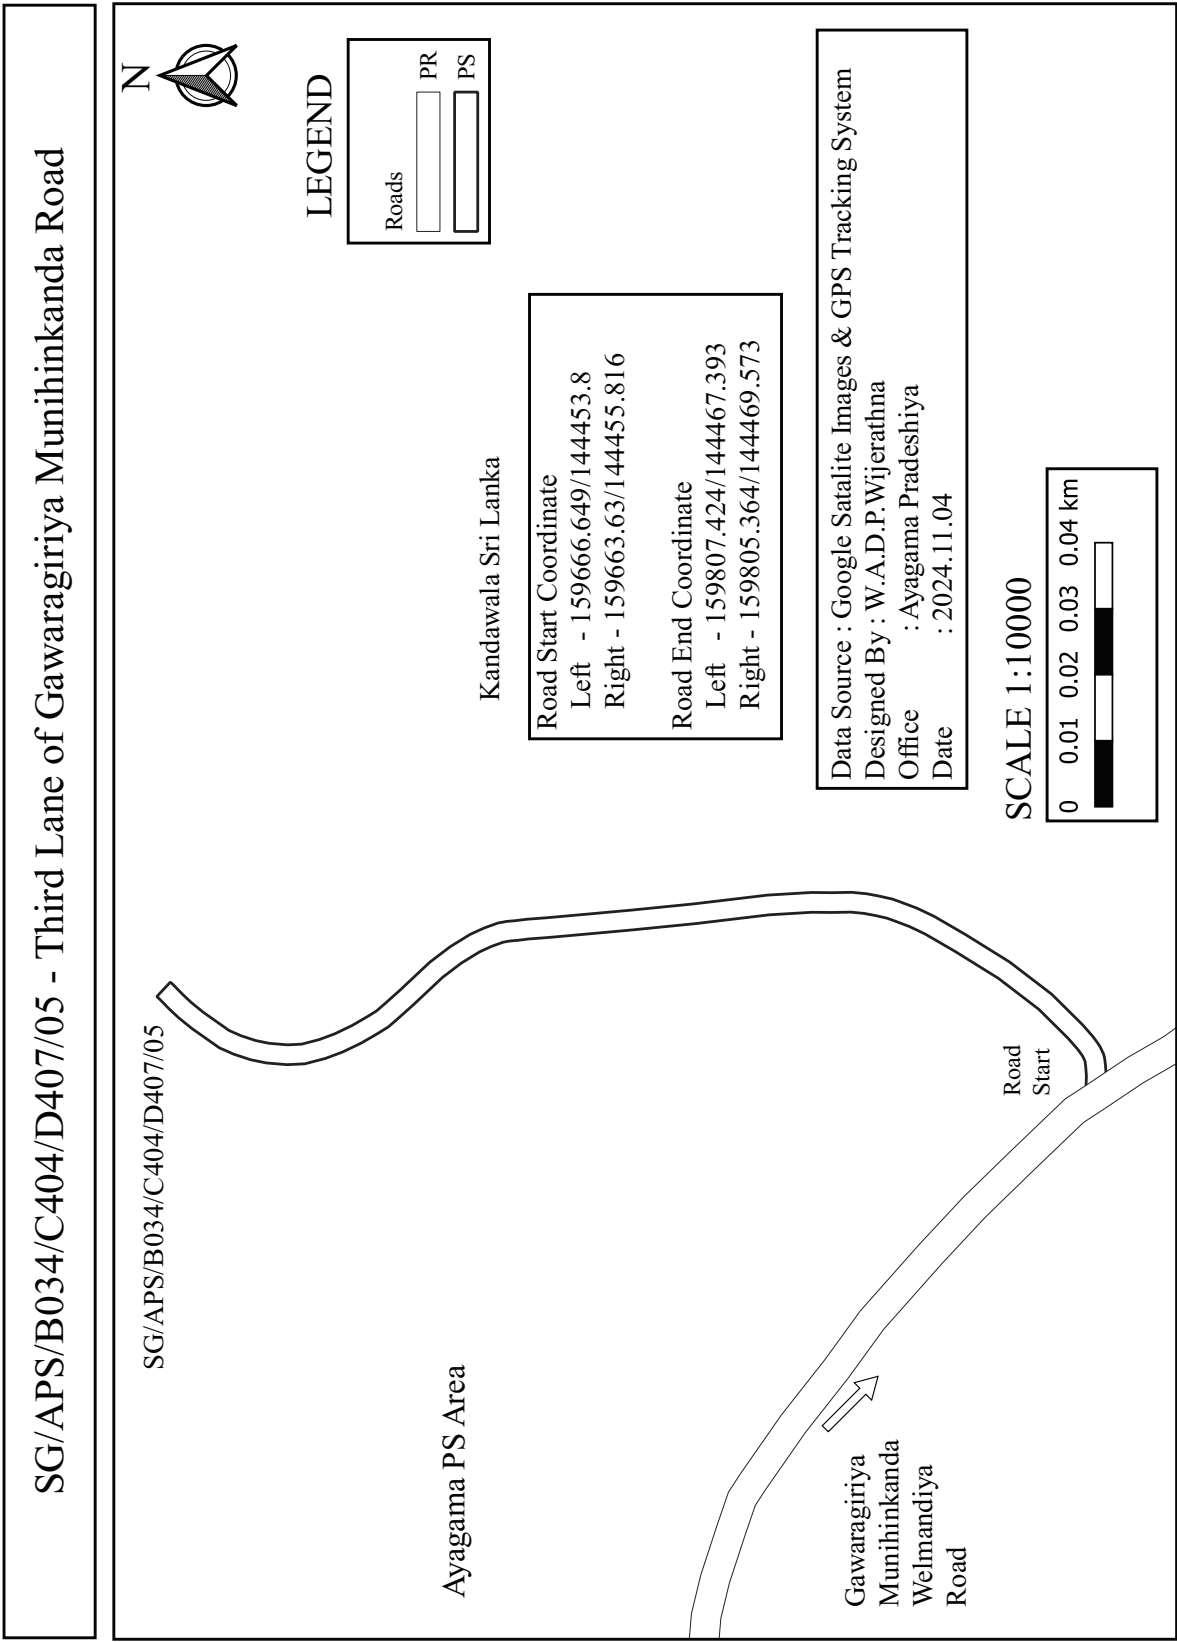








SG/APS/B034/C404/D407/06/01 - First Subway of Fourth Lane of Gawaragiriya Munihinkanda Road

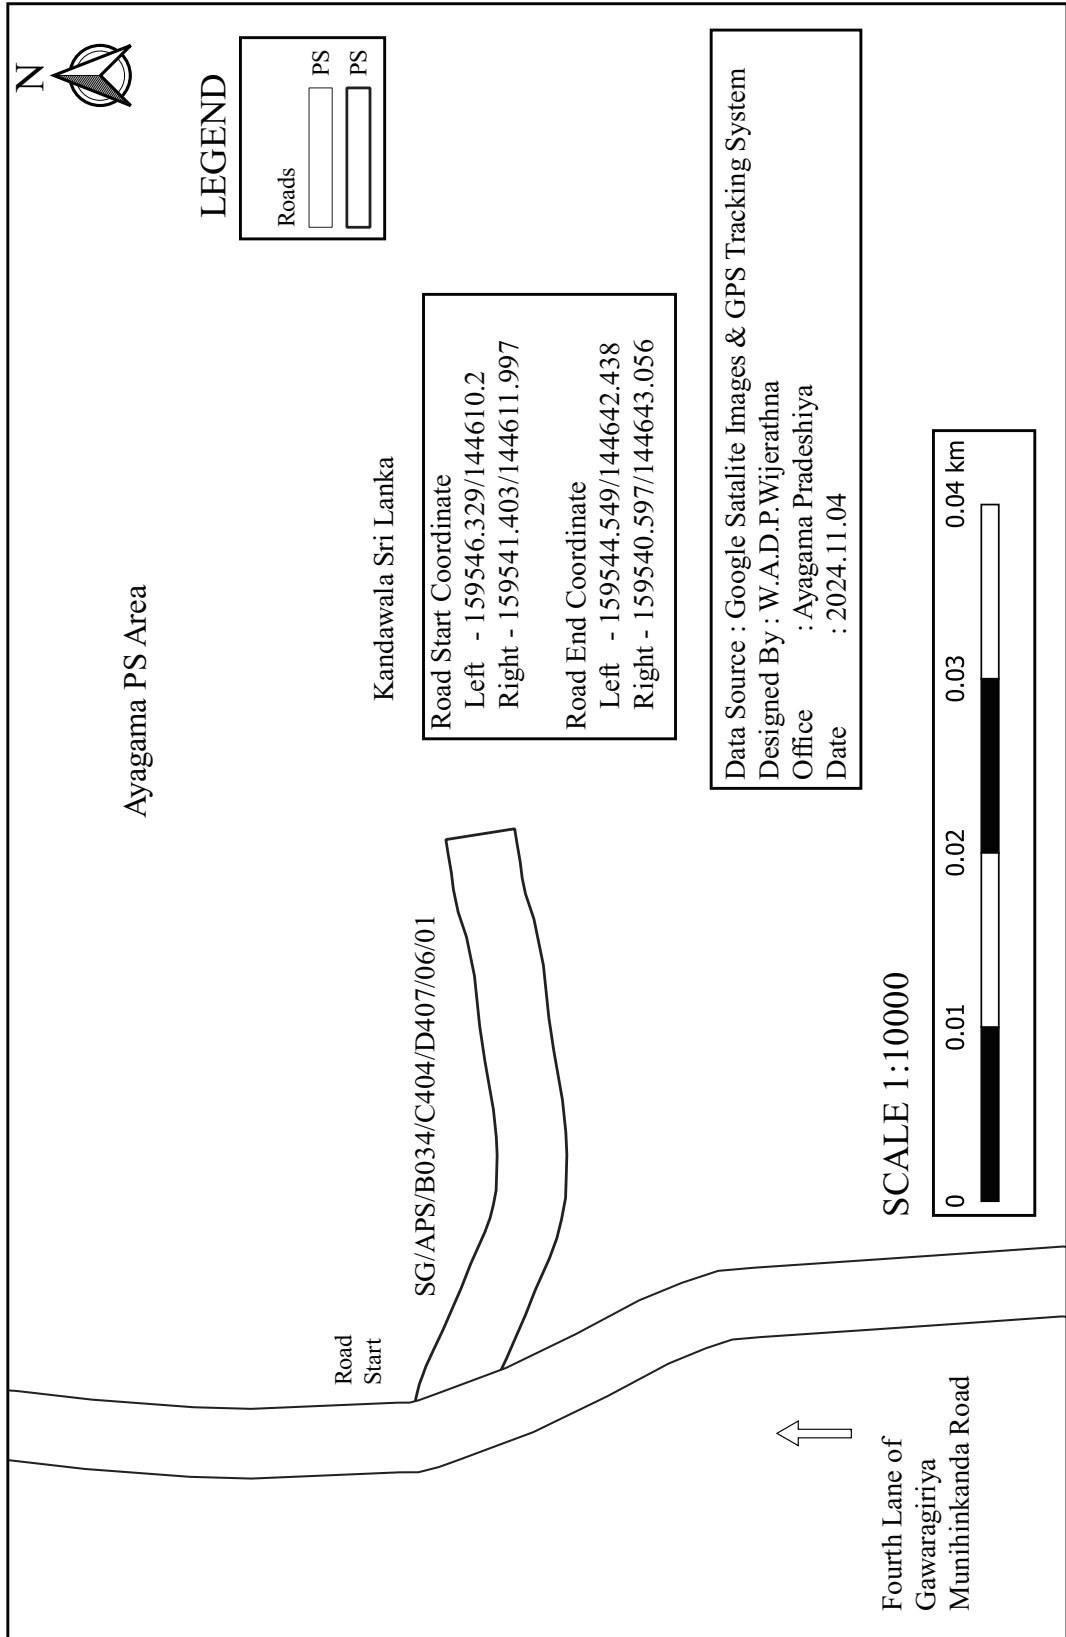


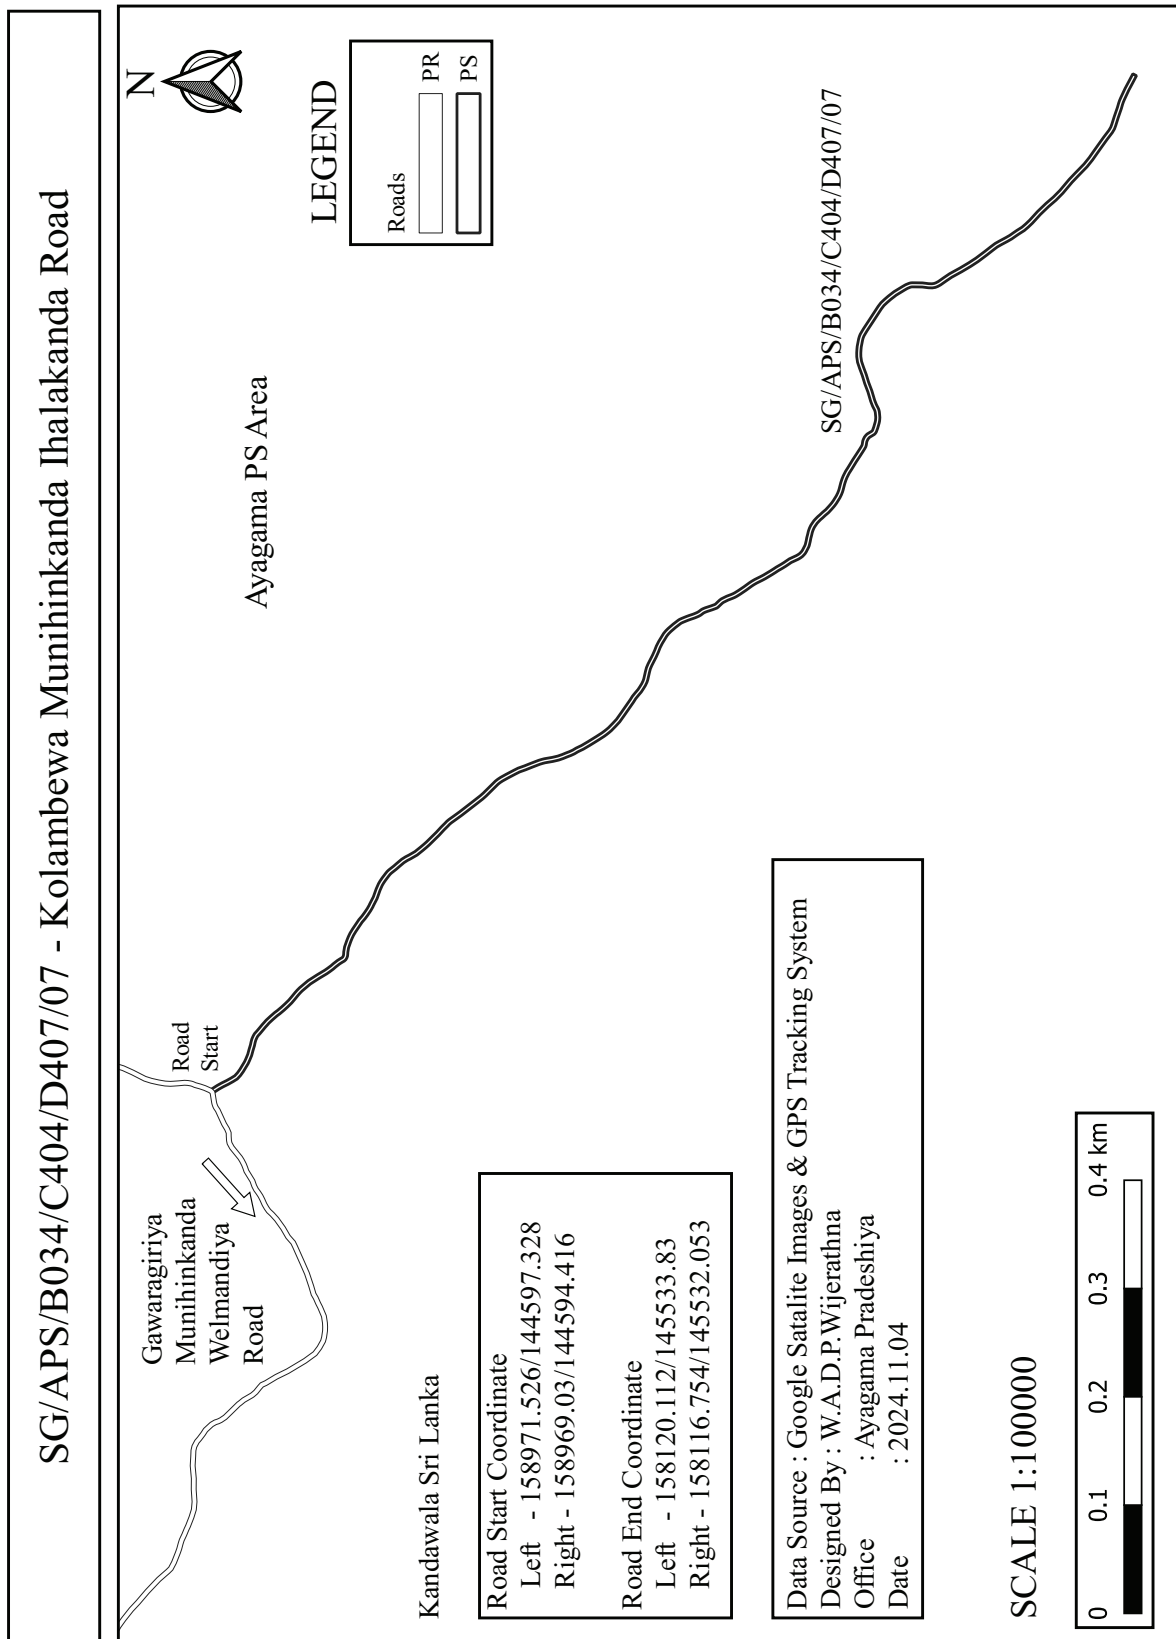


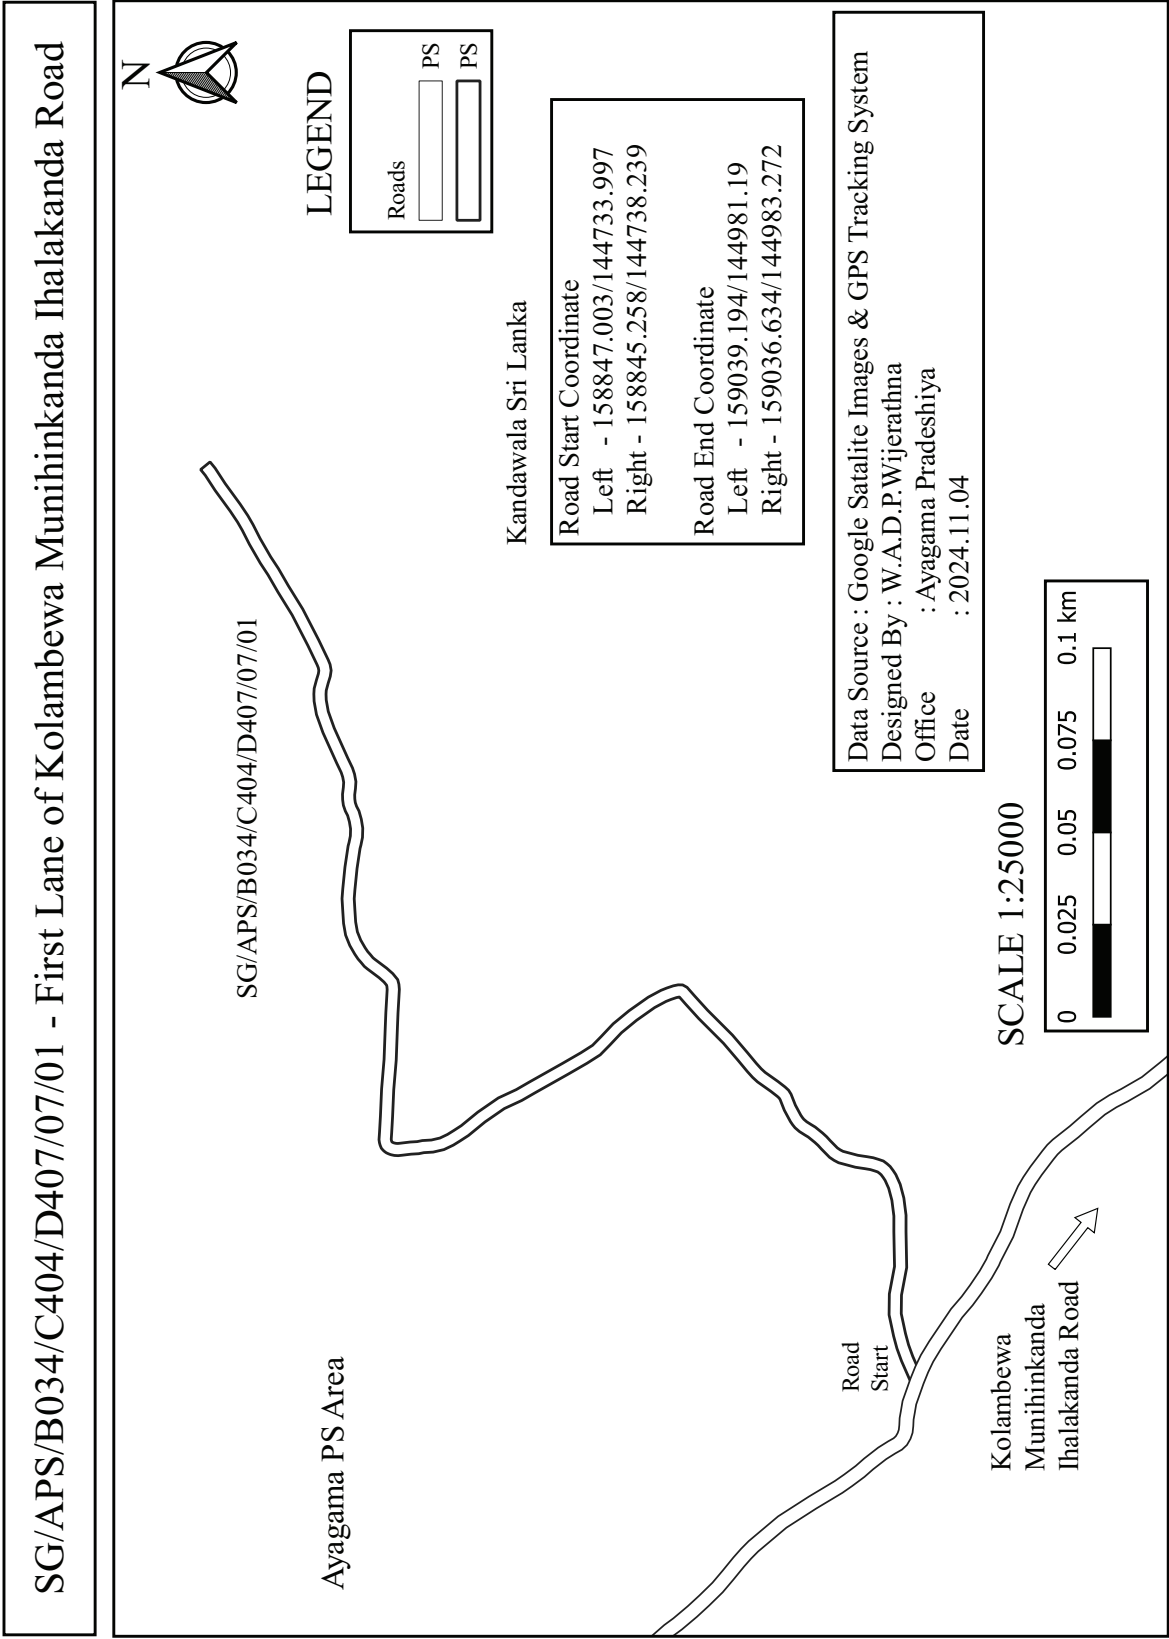


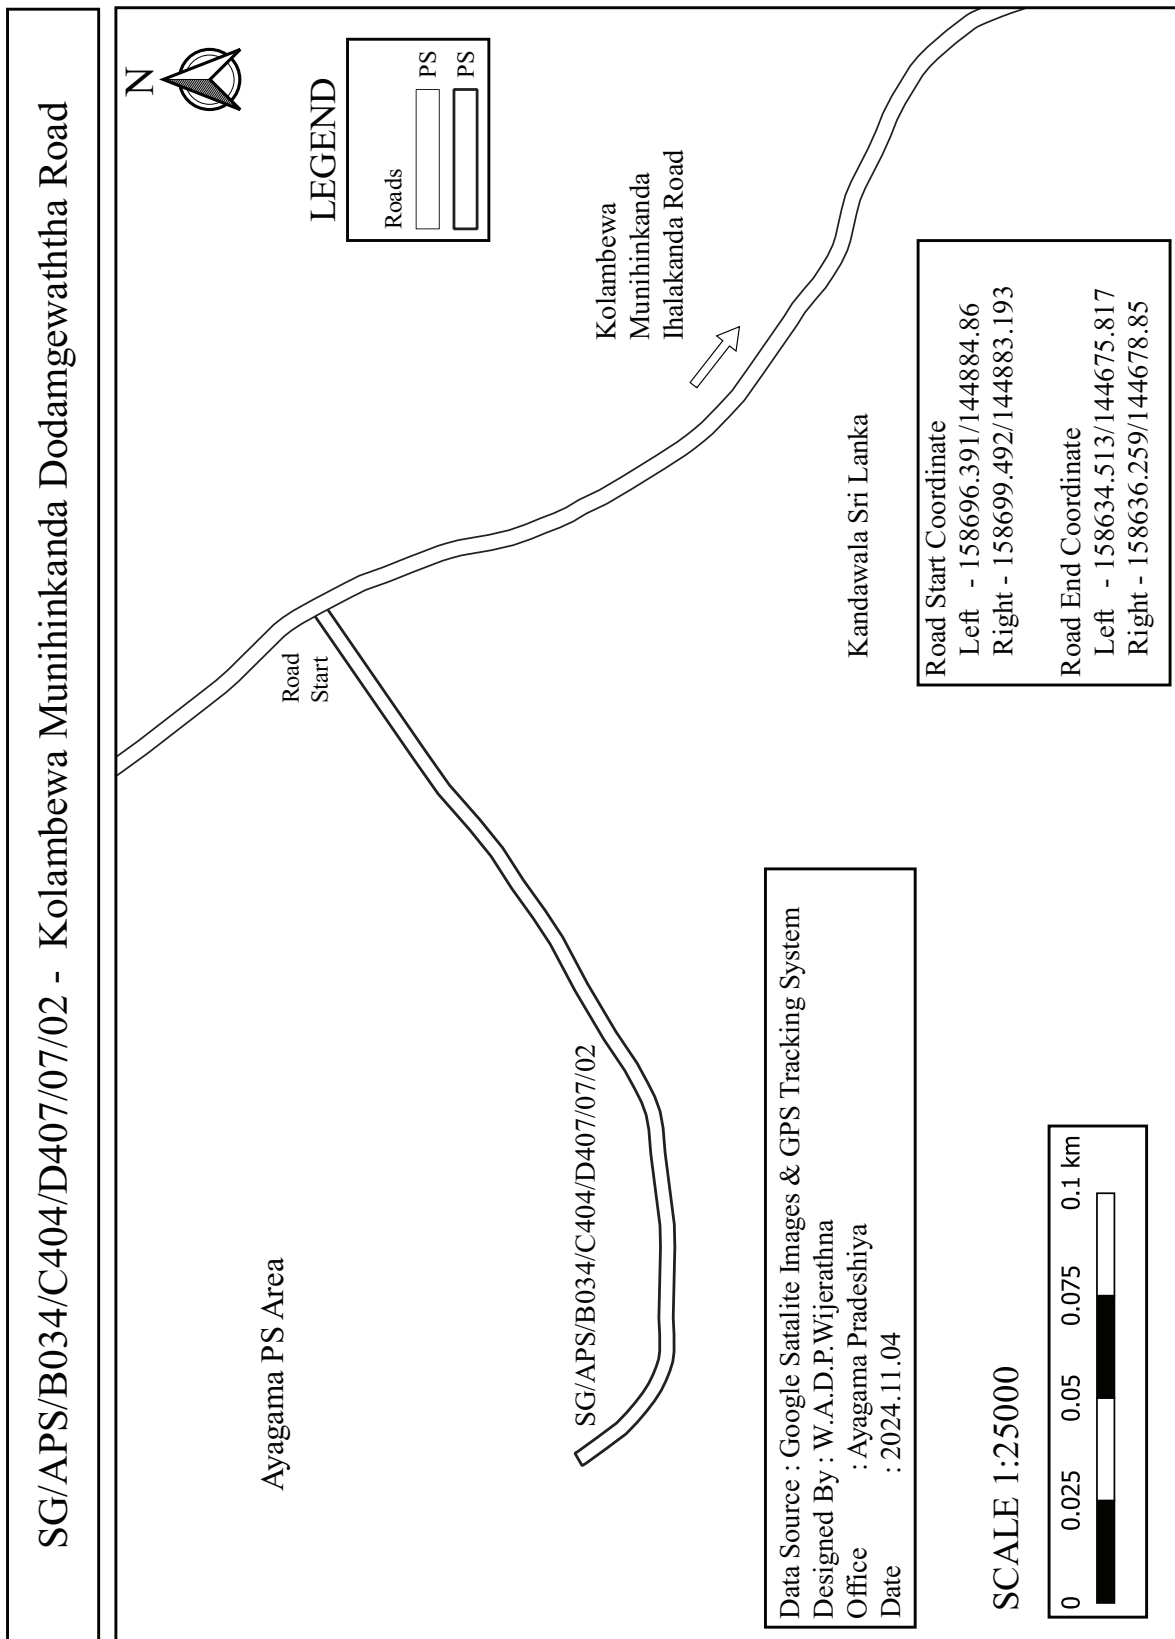


SG/APS/B034/C404/D407/07/03 - Fifth Lane of Kolambewa Munihinkanda

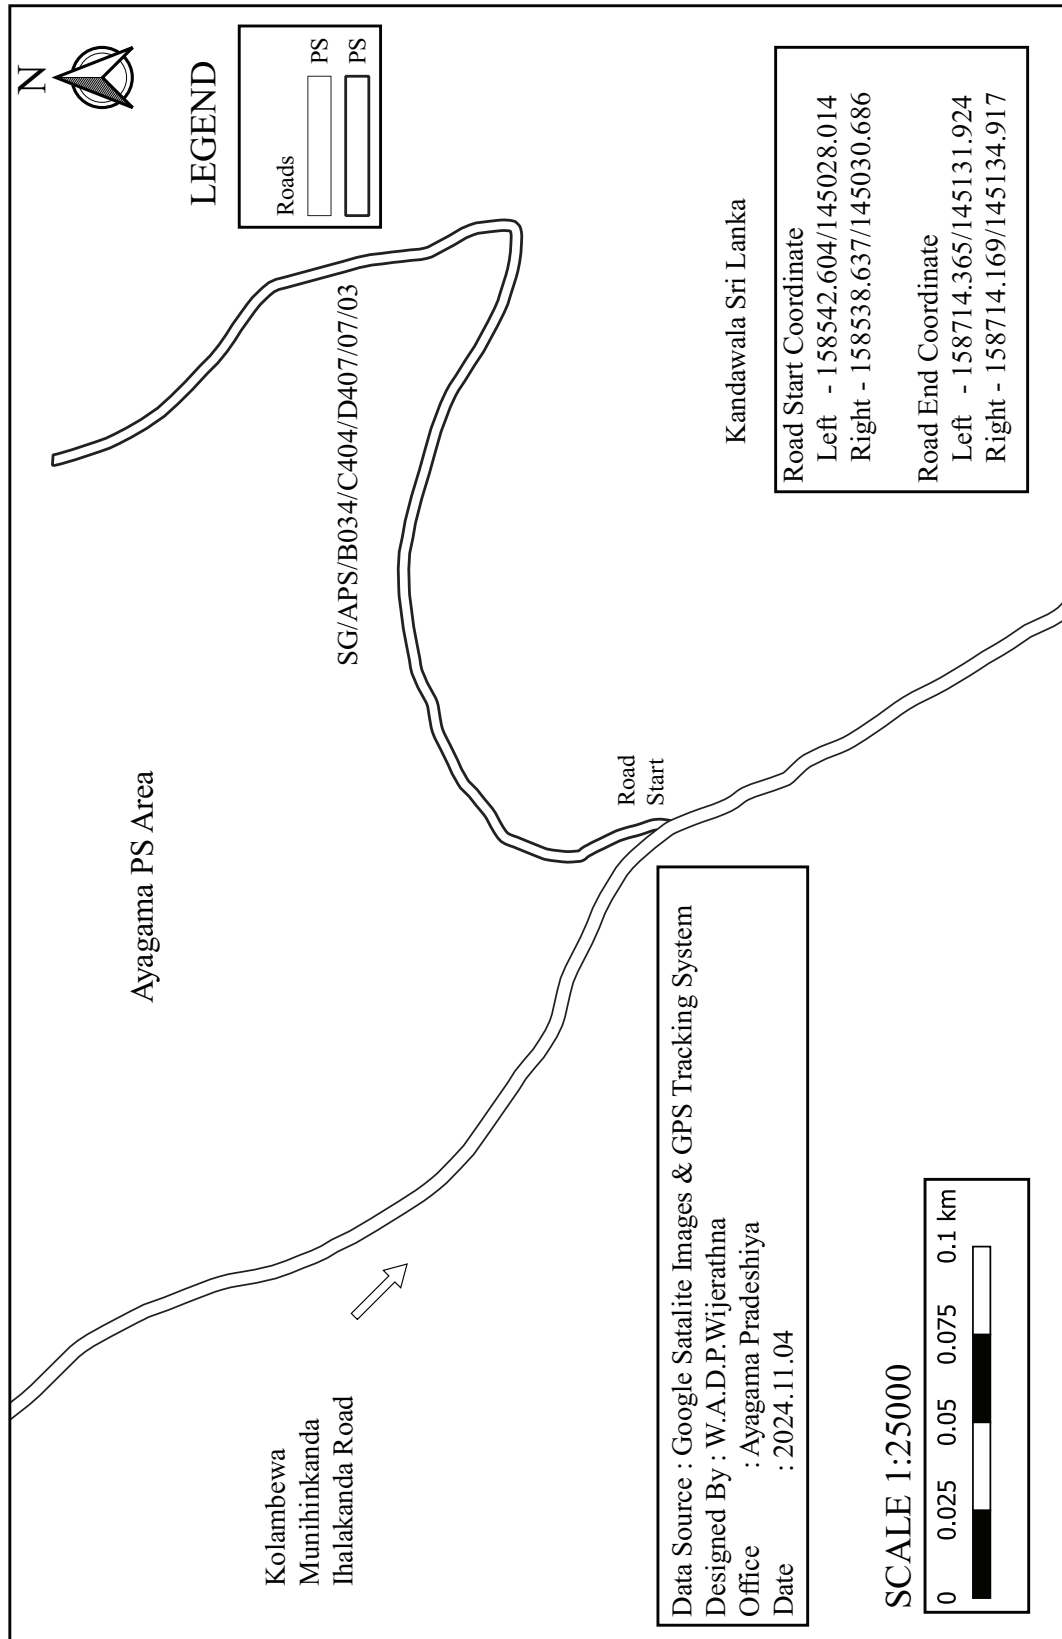


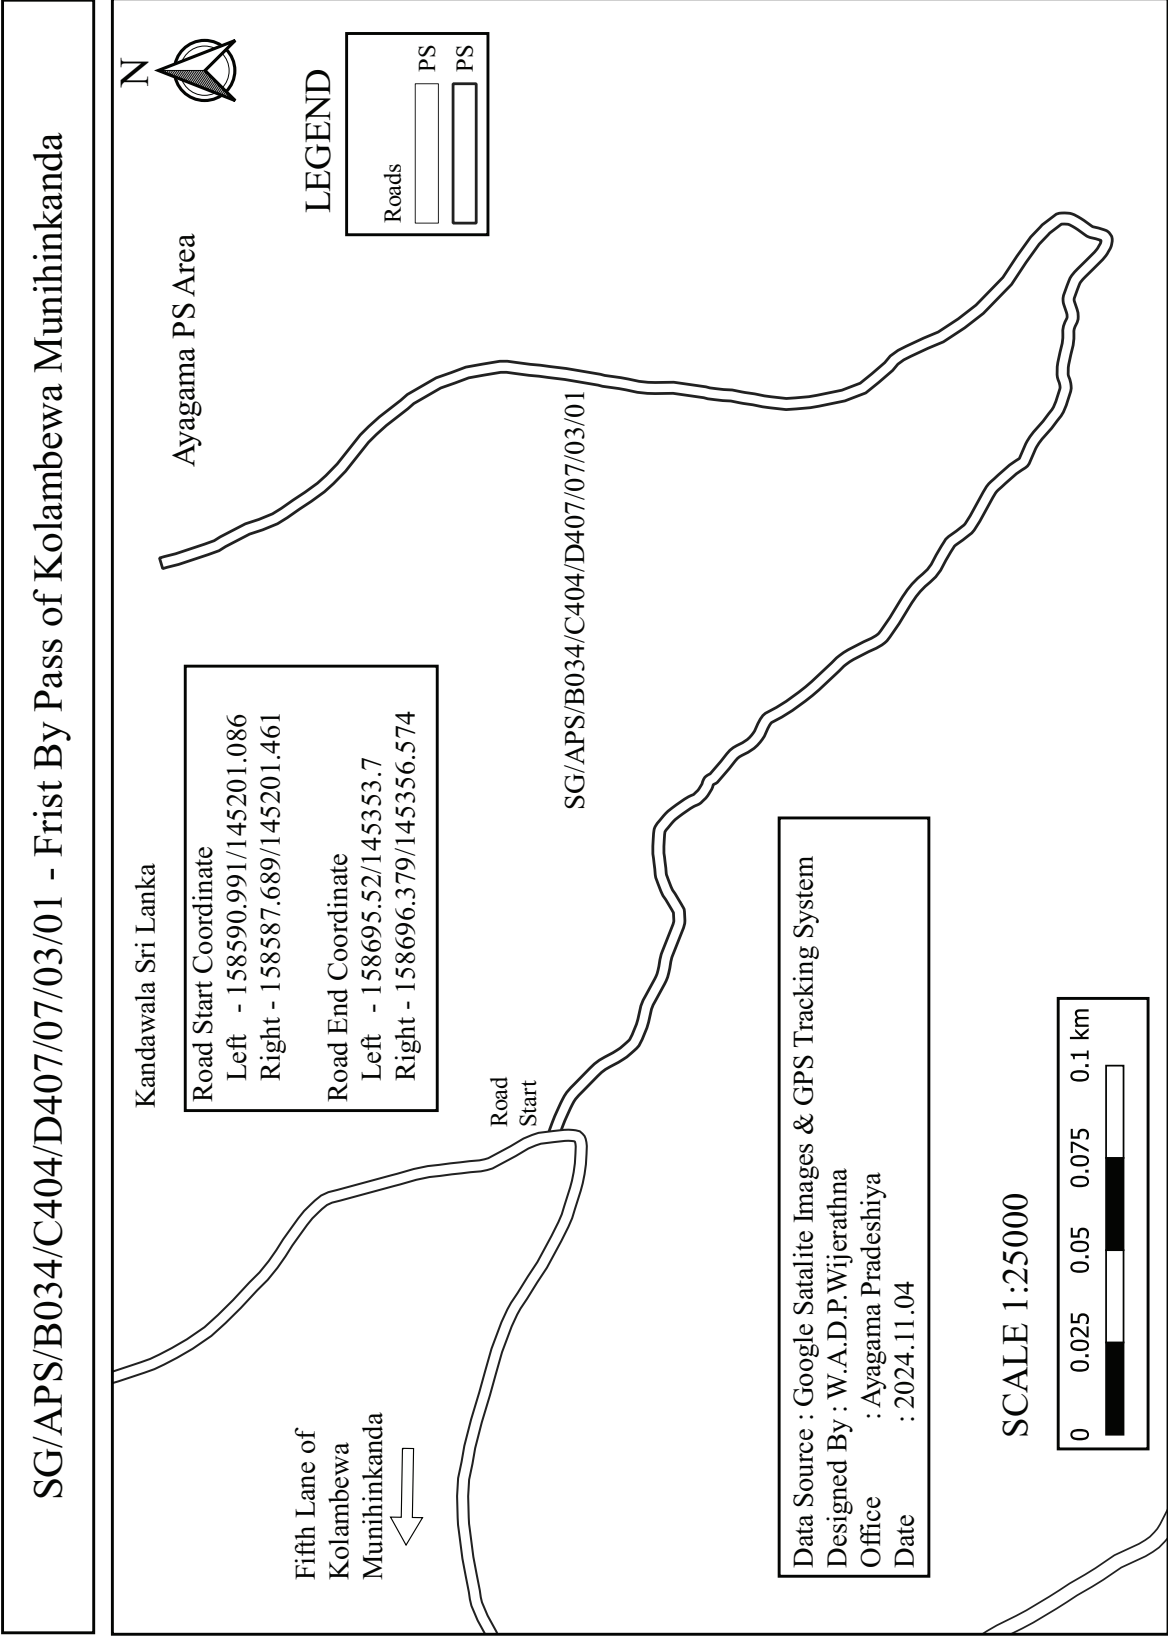


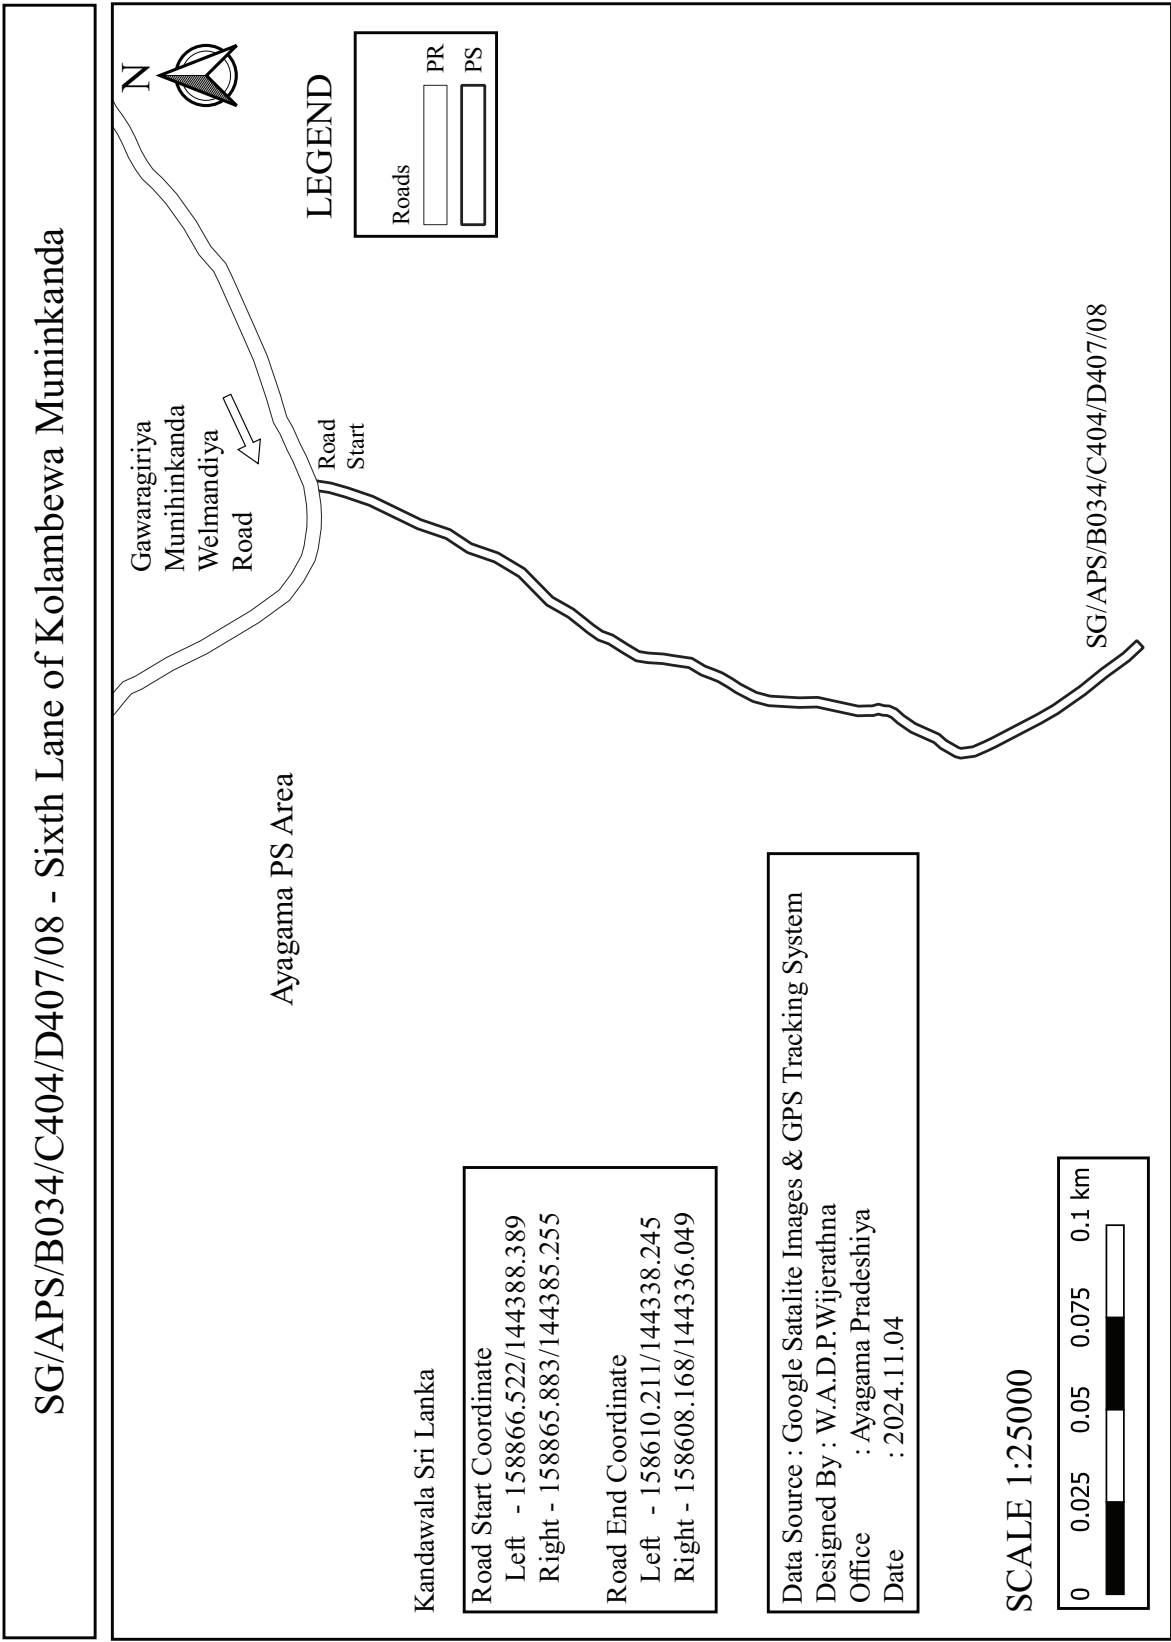


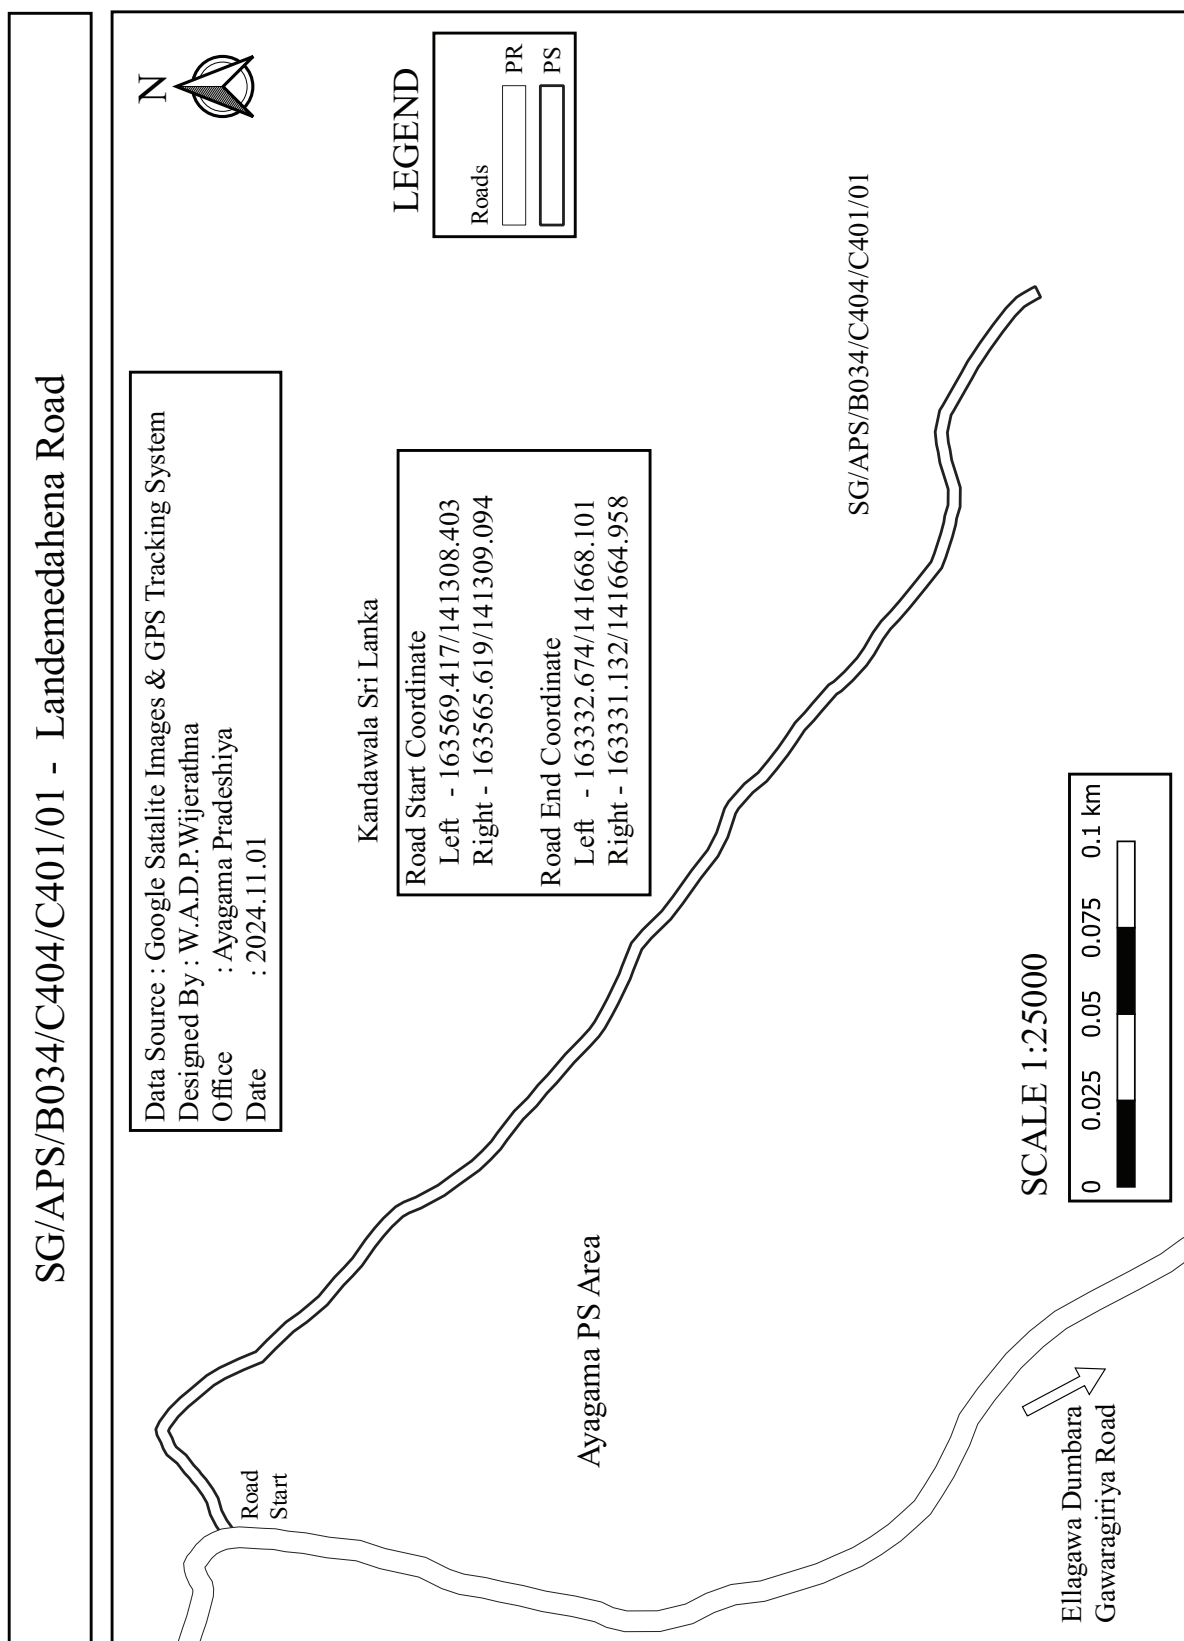




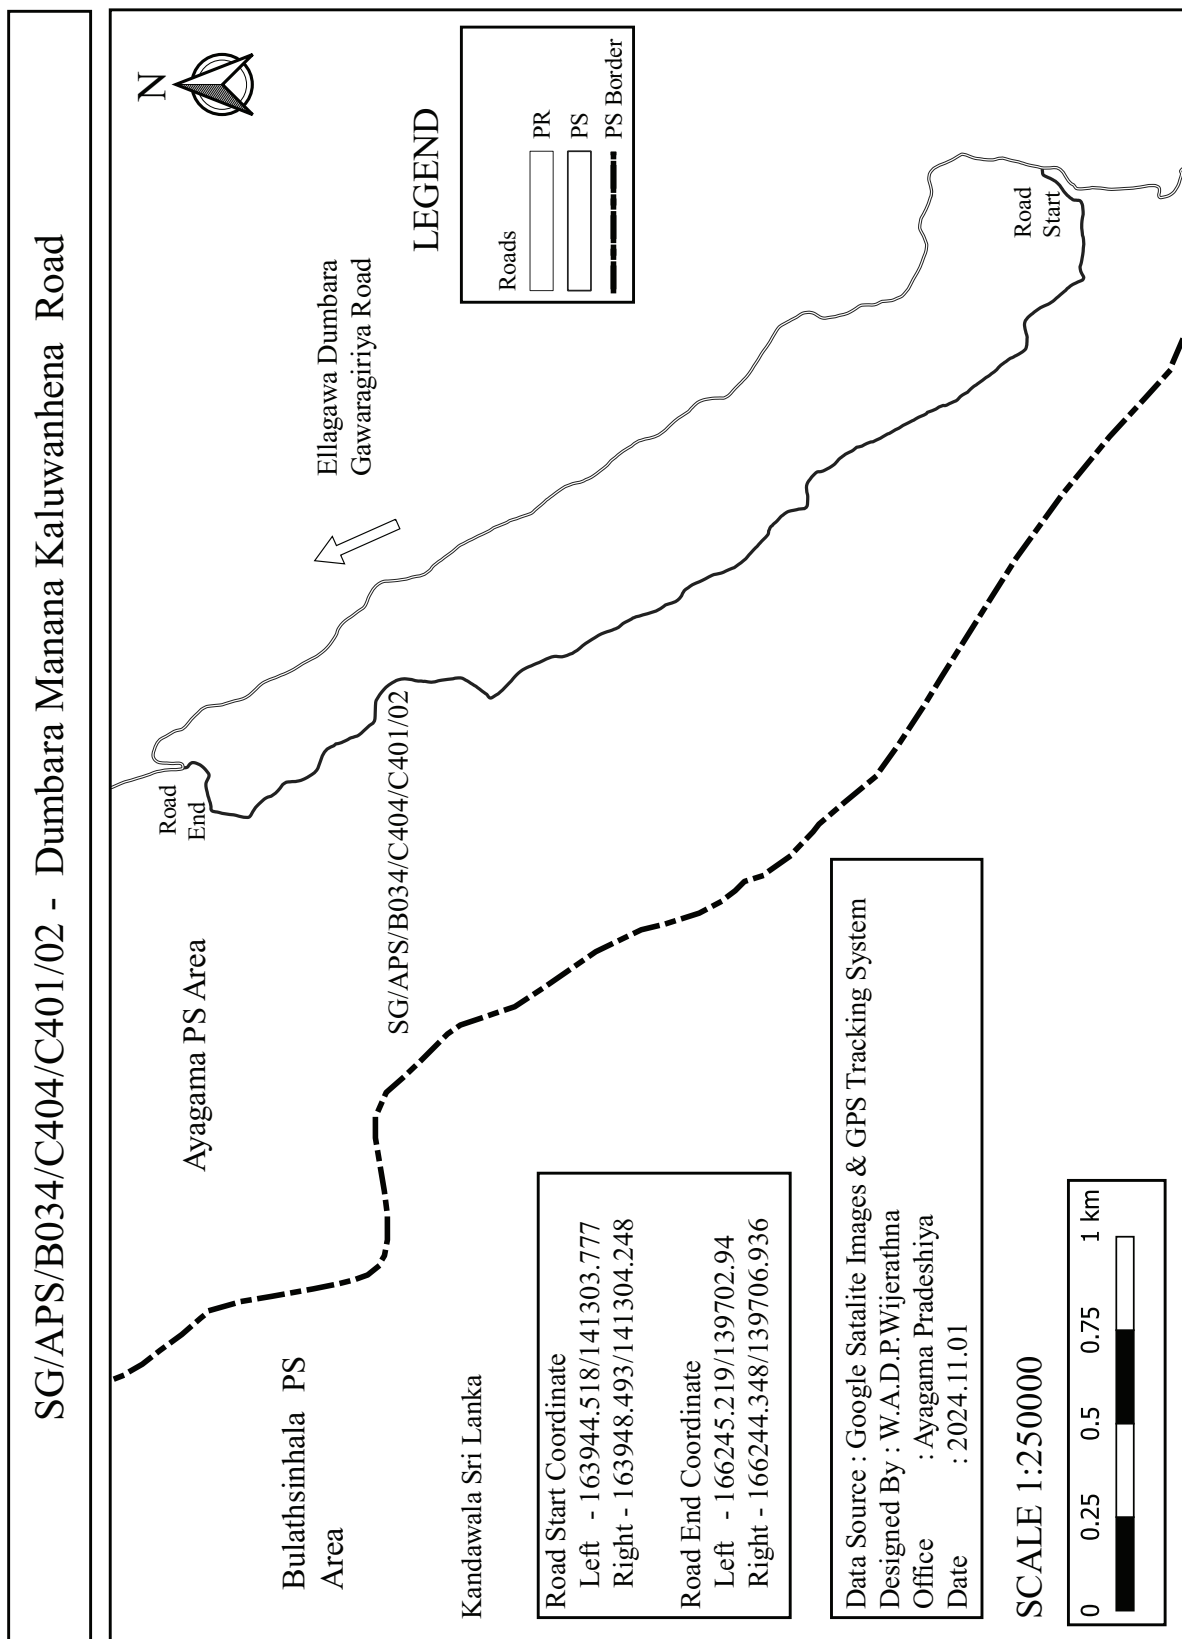


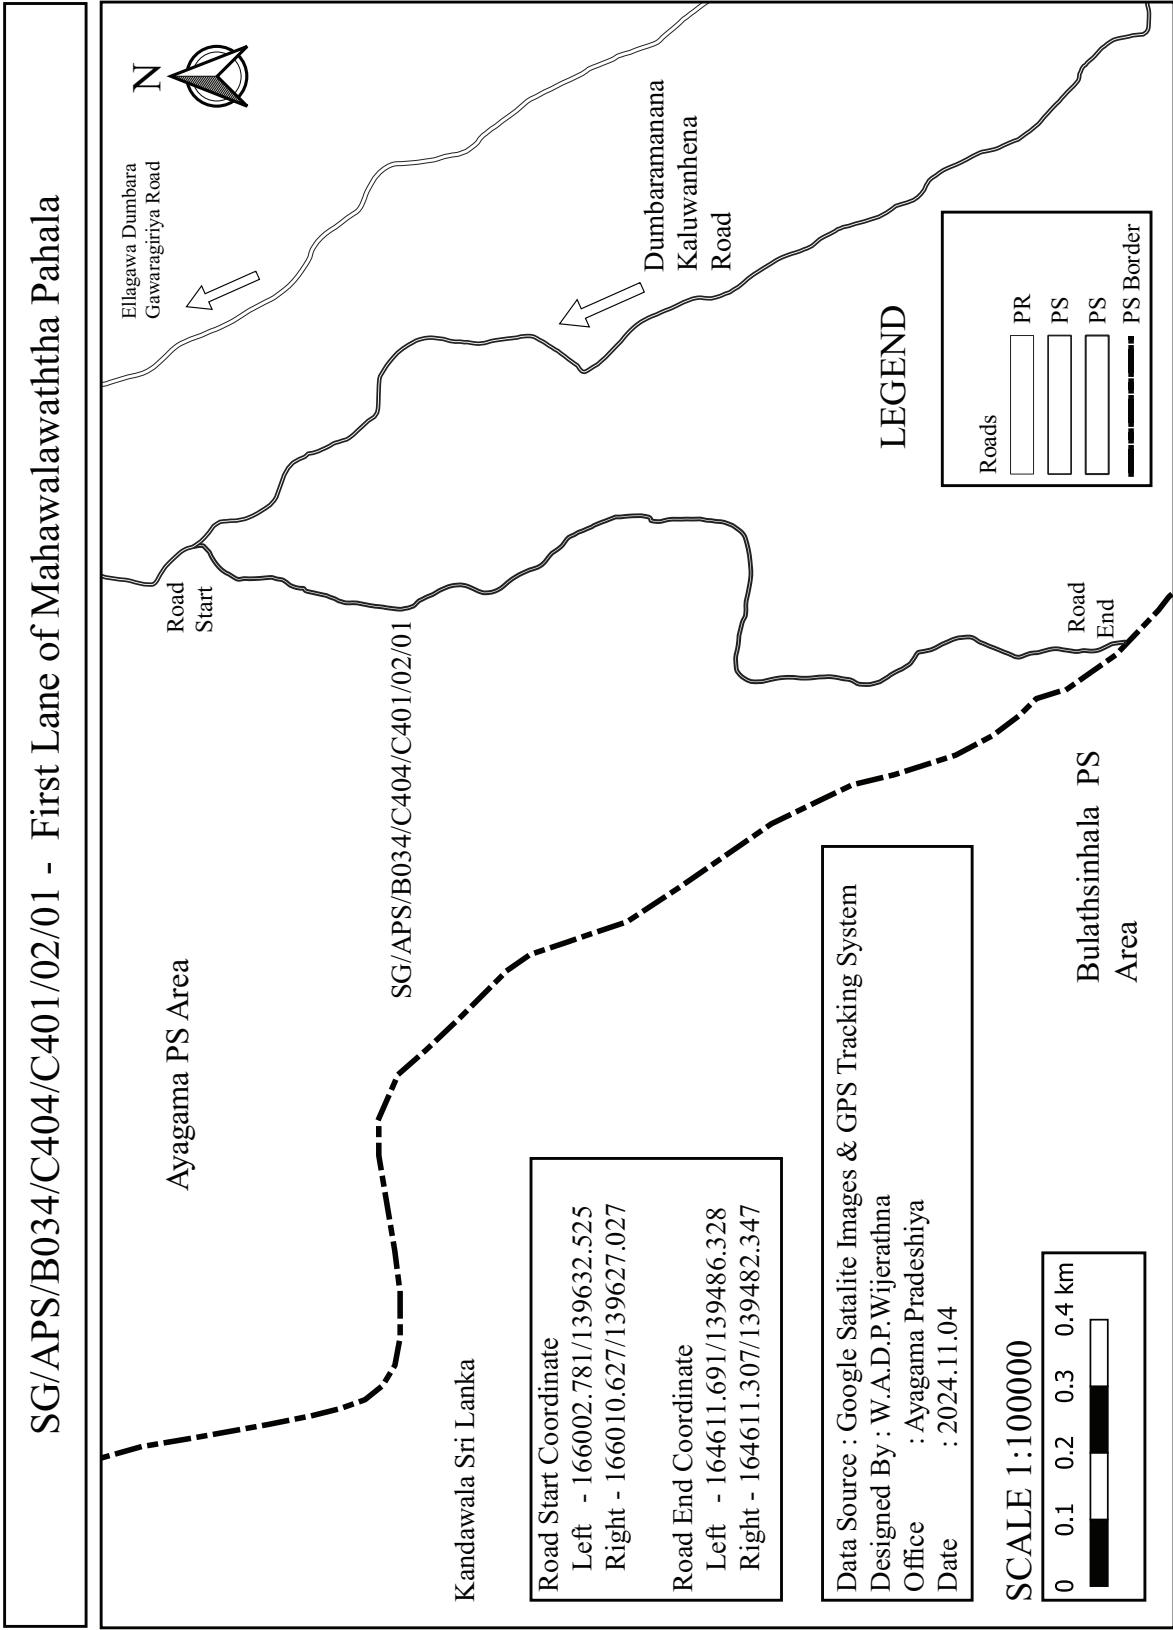


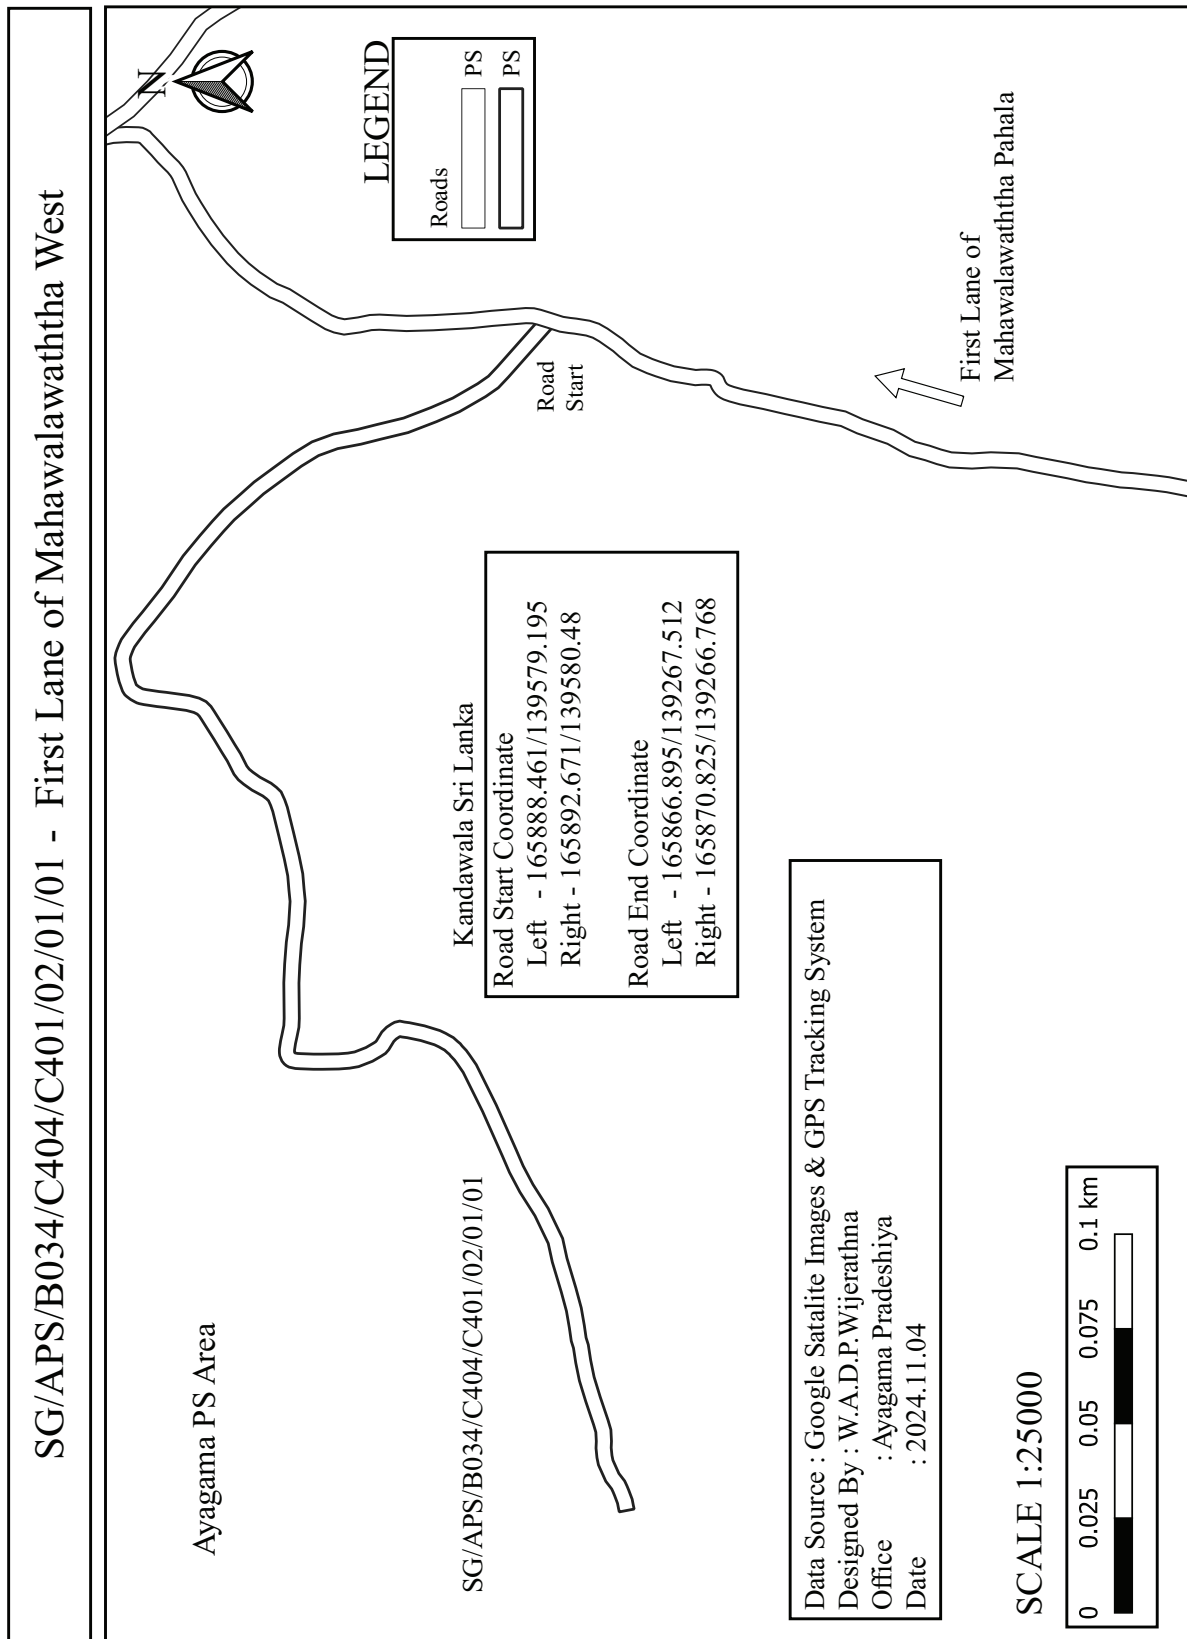


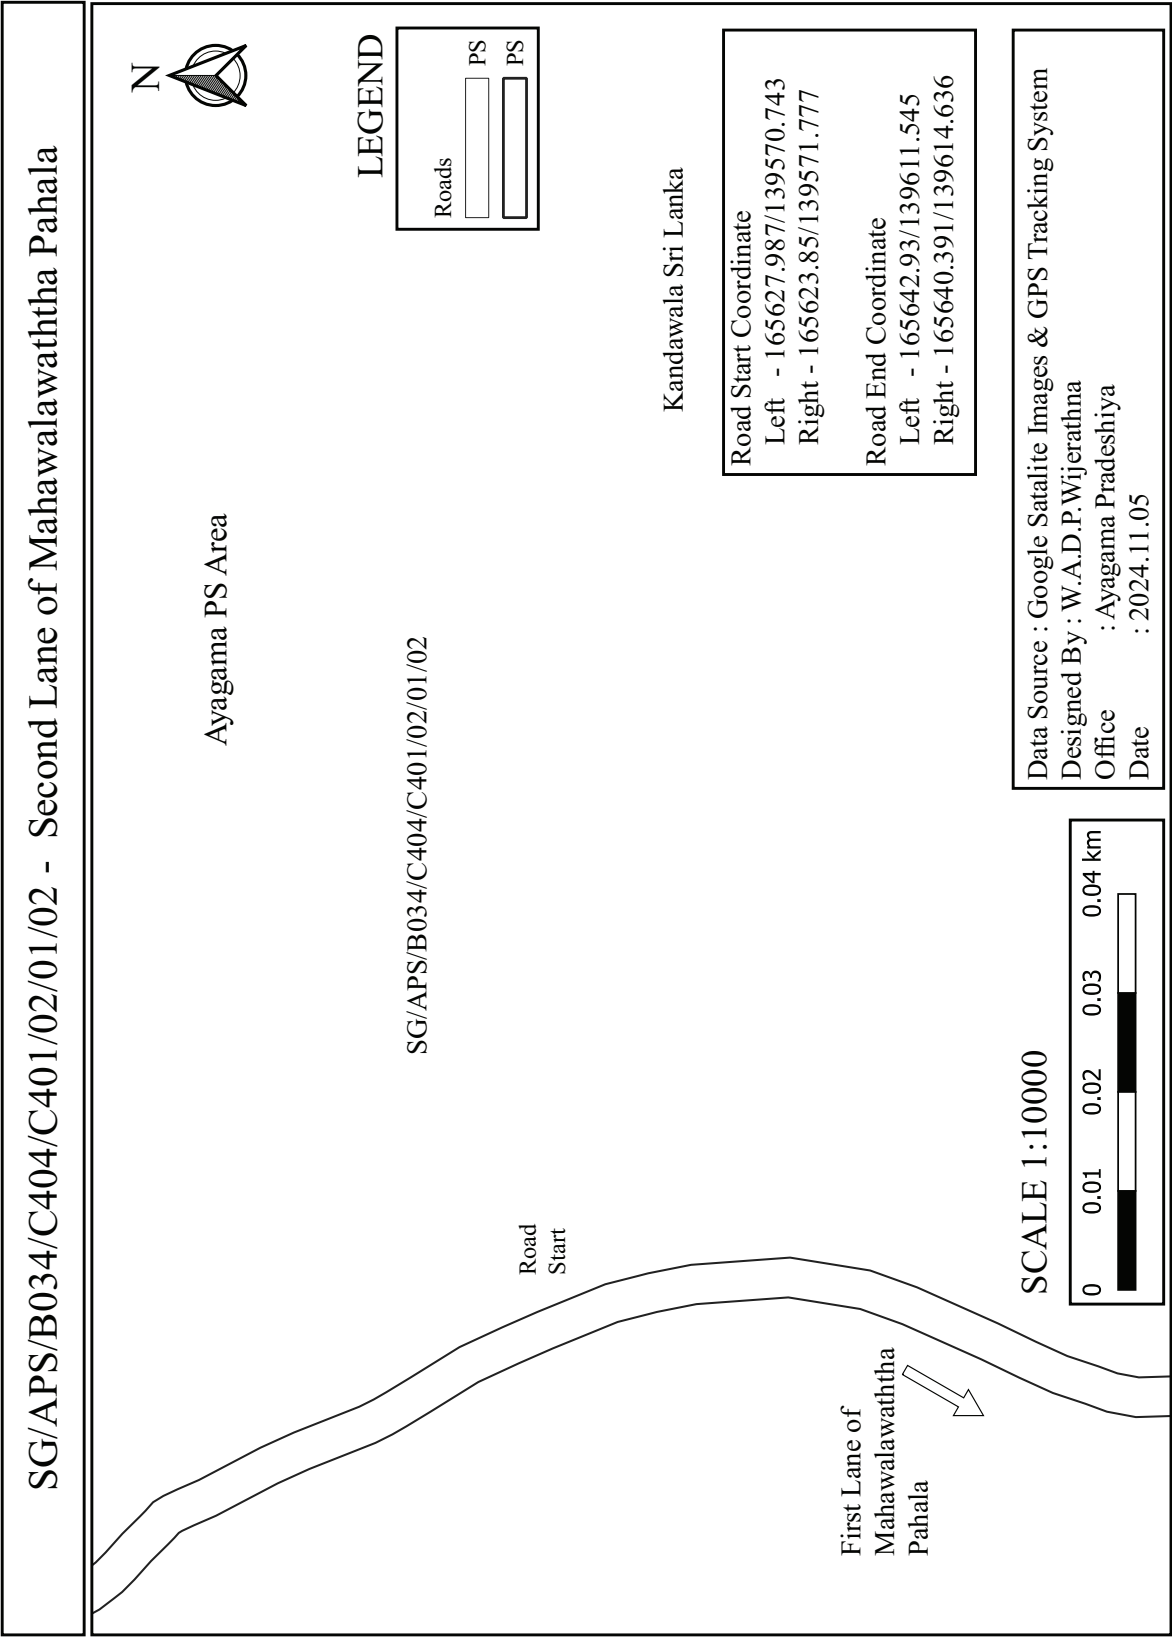


SG/APS/B034/C404/C401/02/01/03 - Second Lane of Mahawalawaththa West

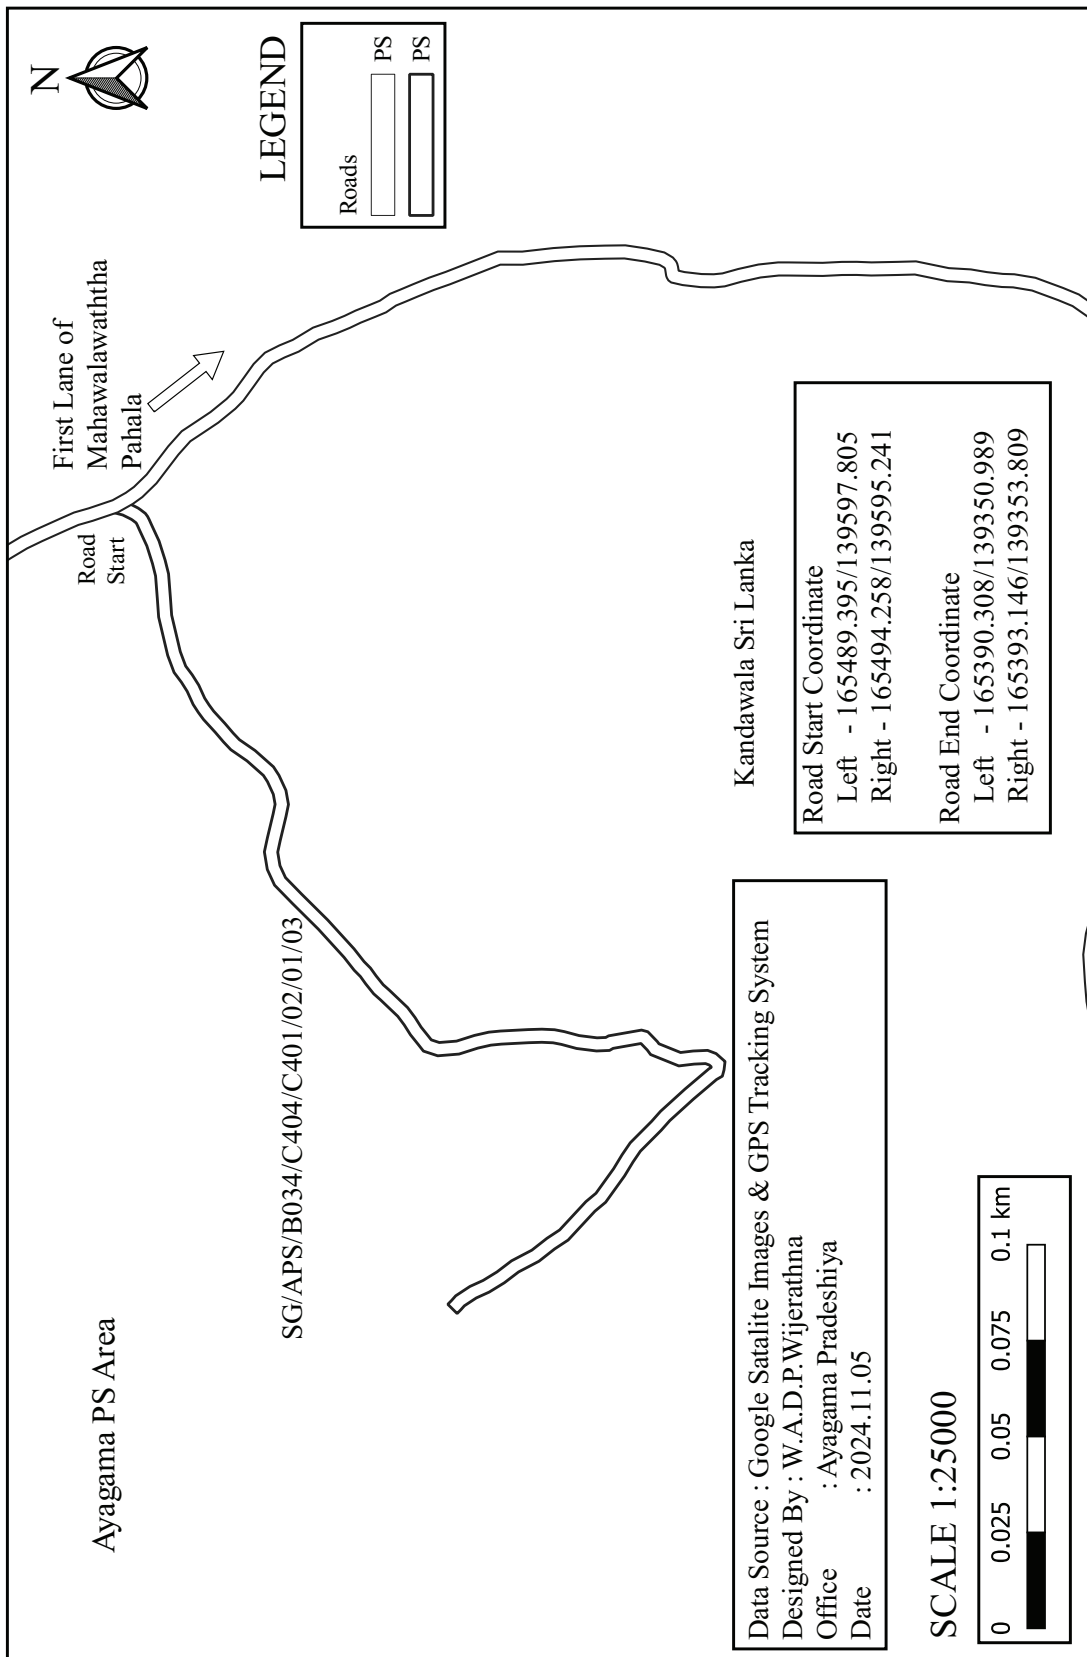


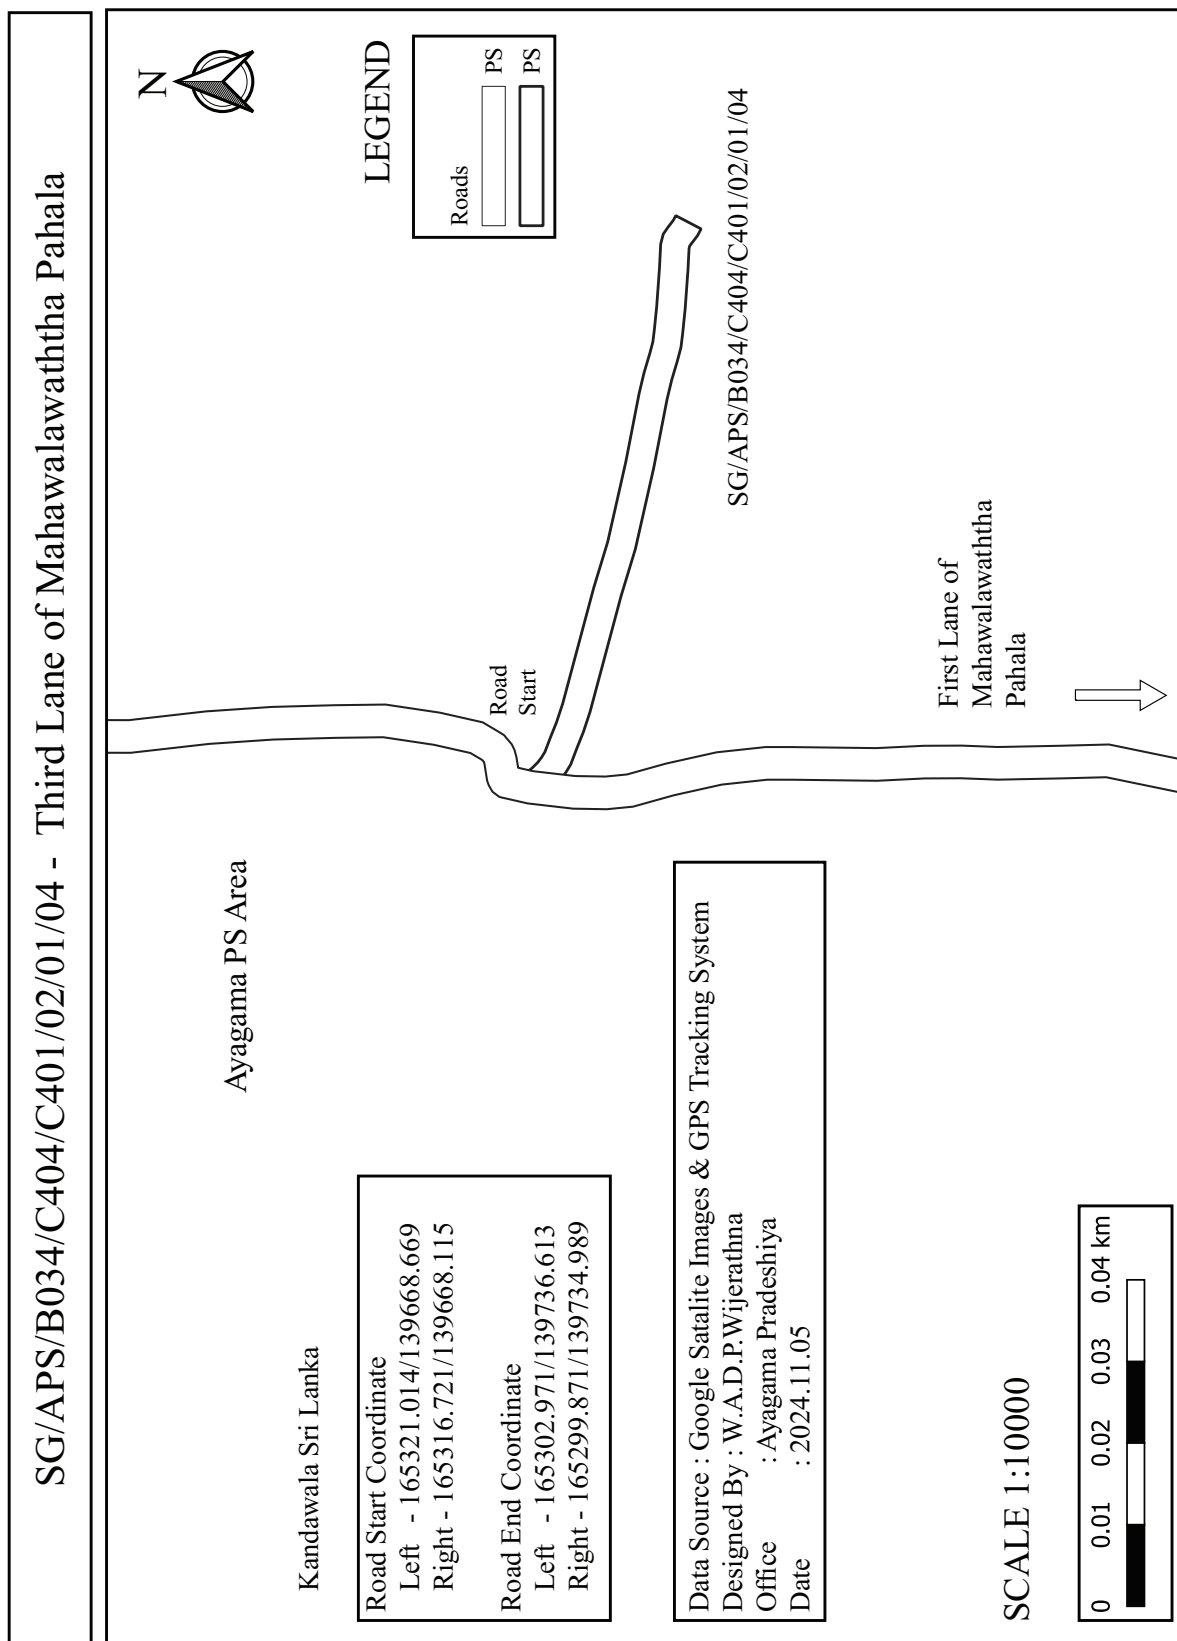


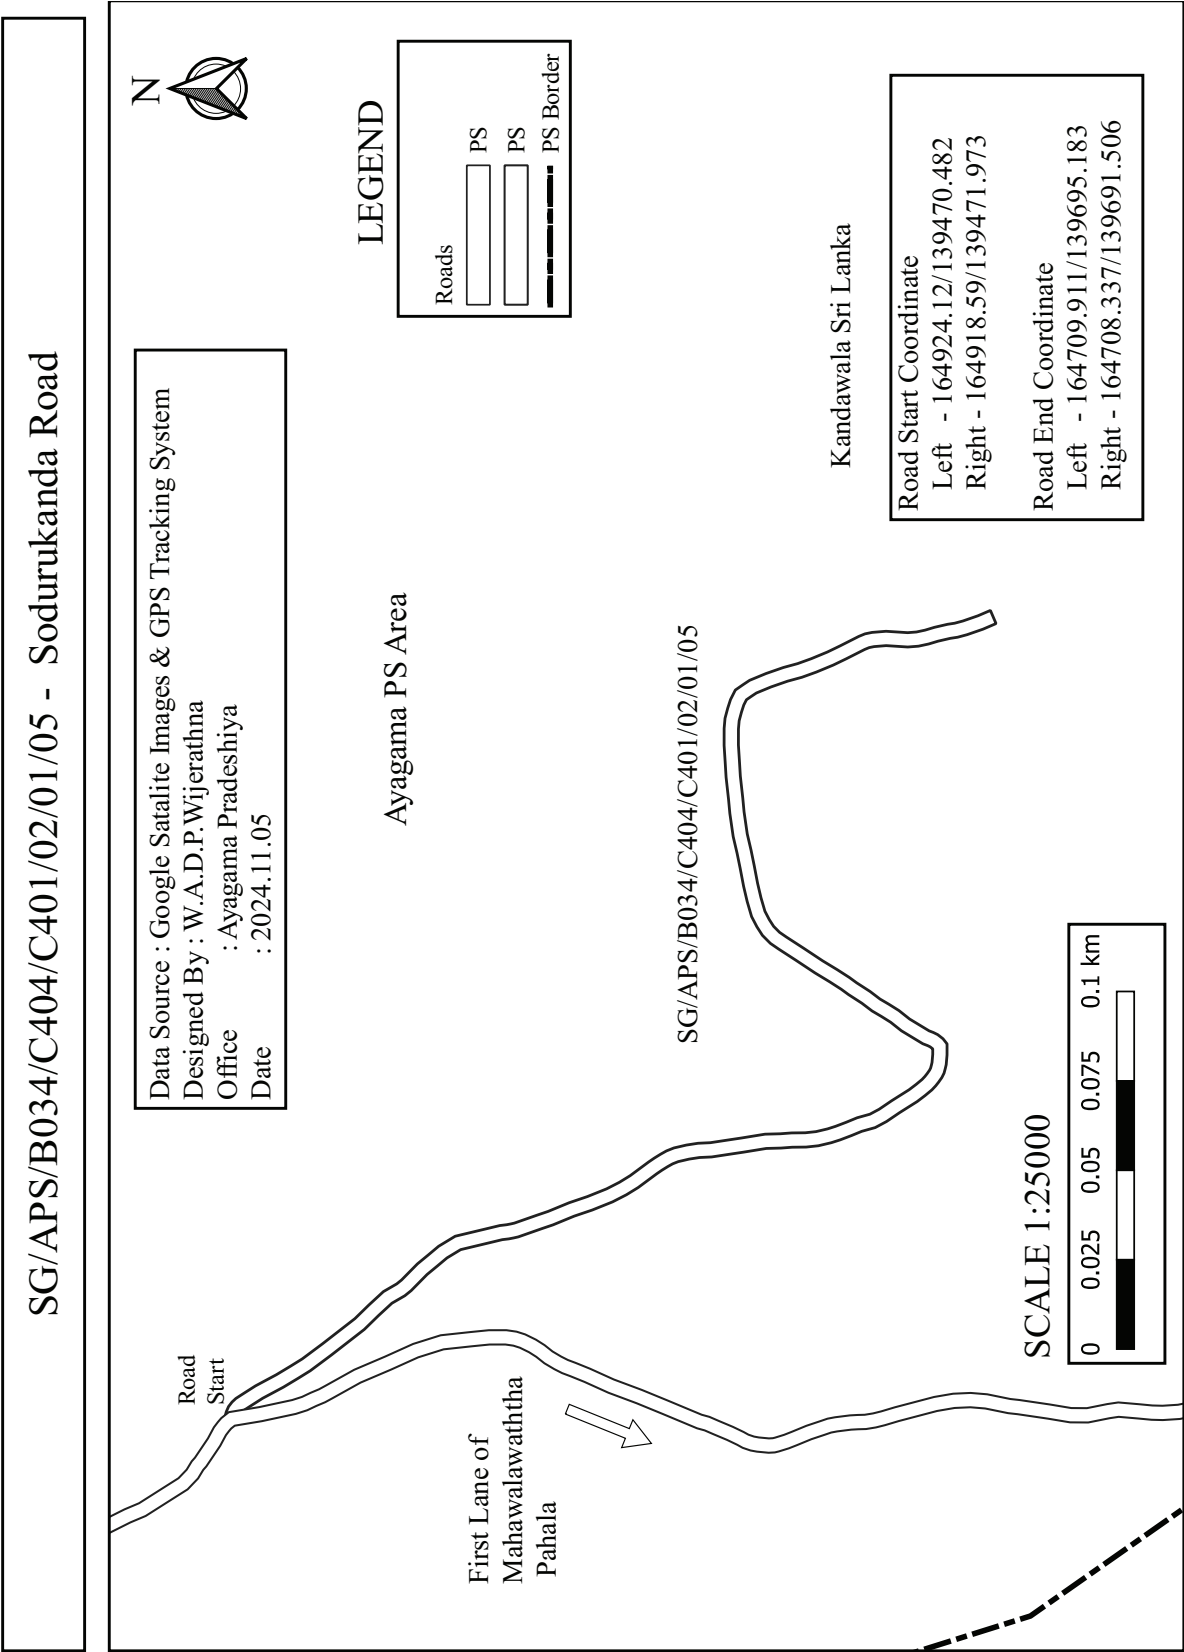


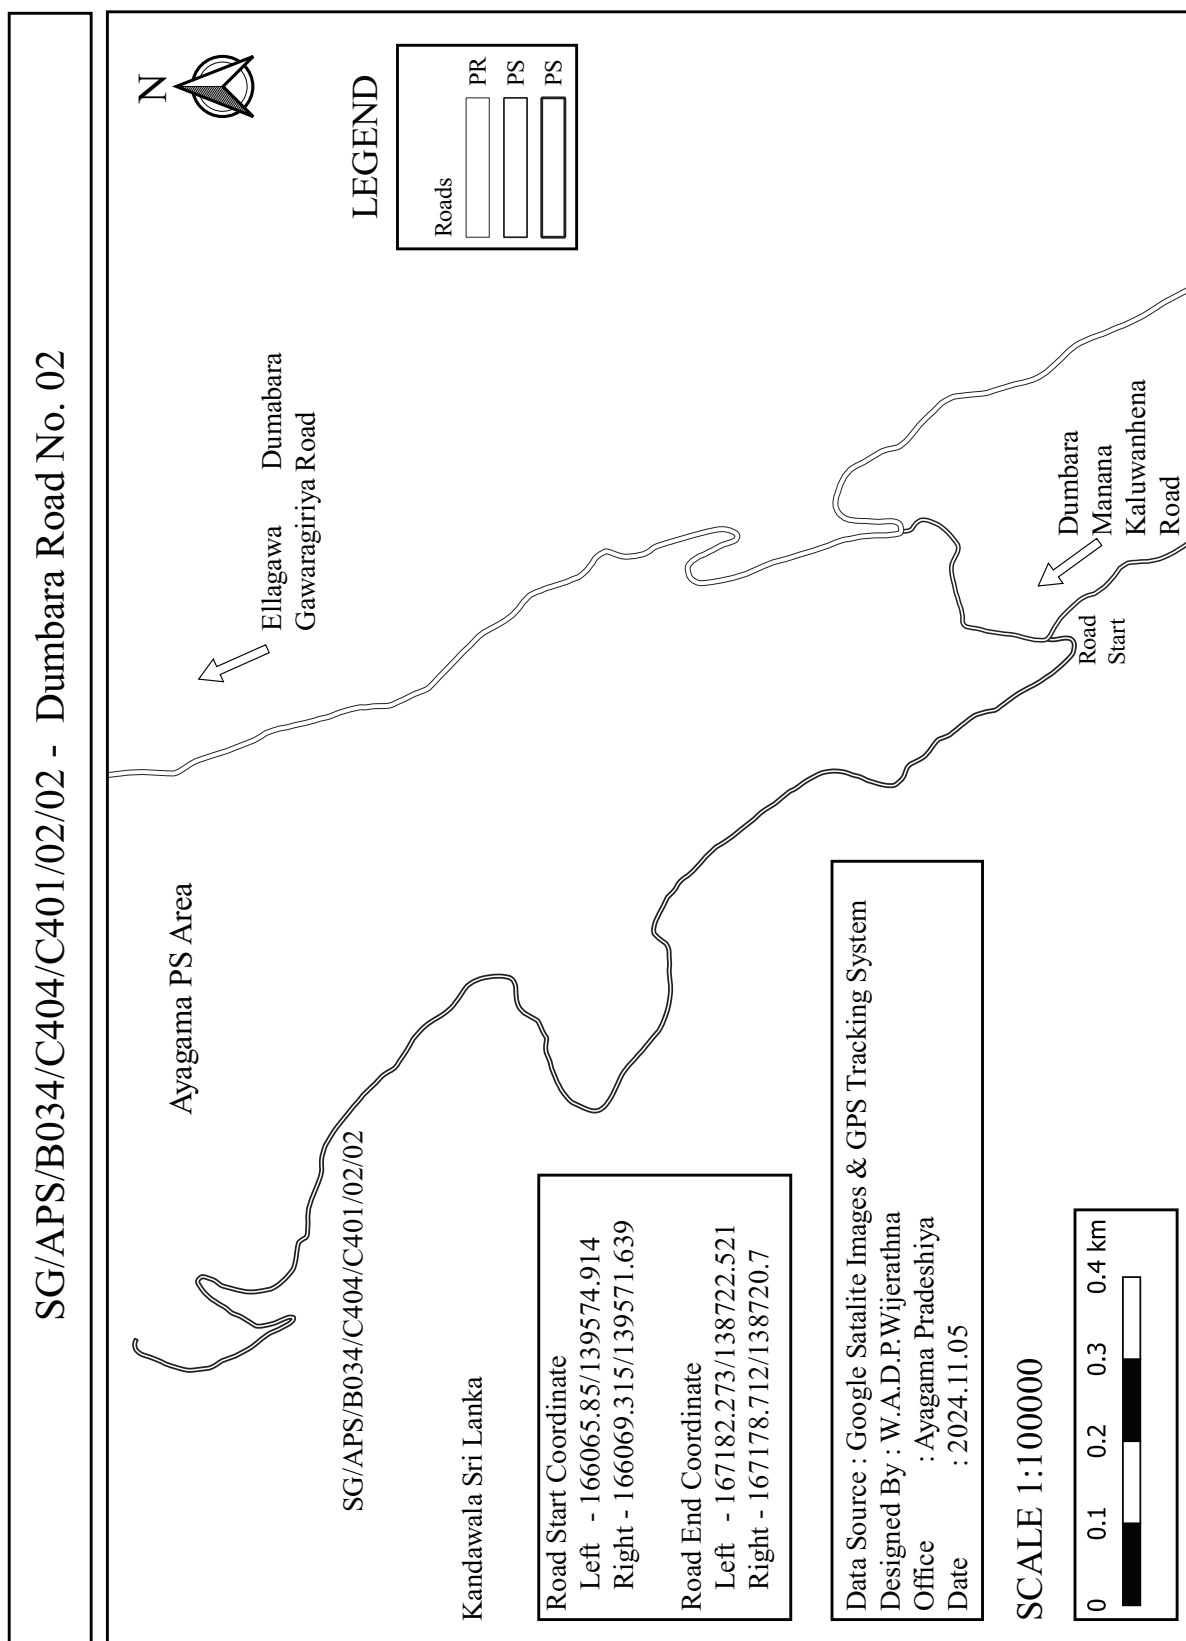





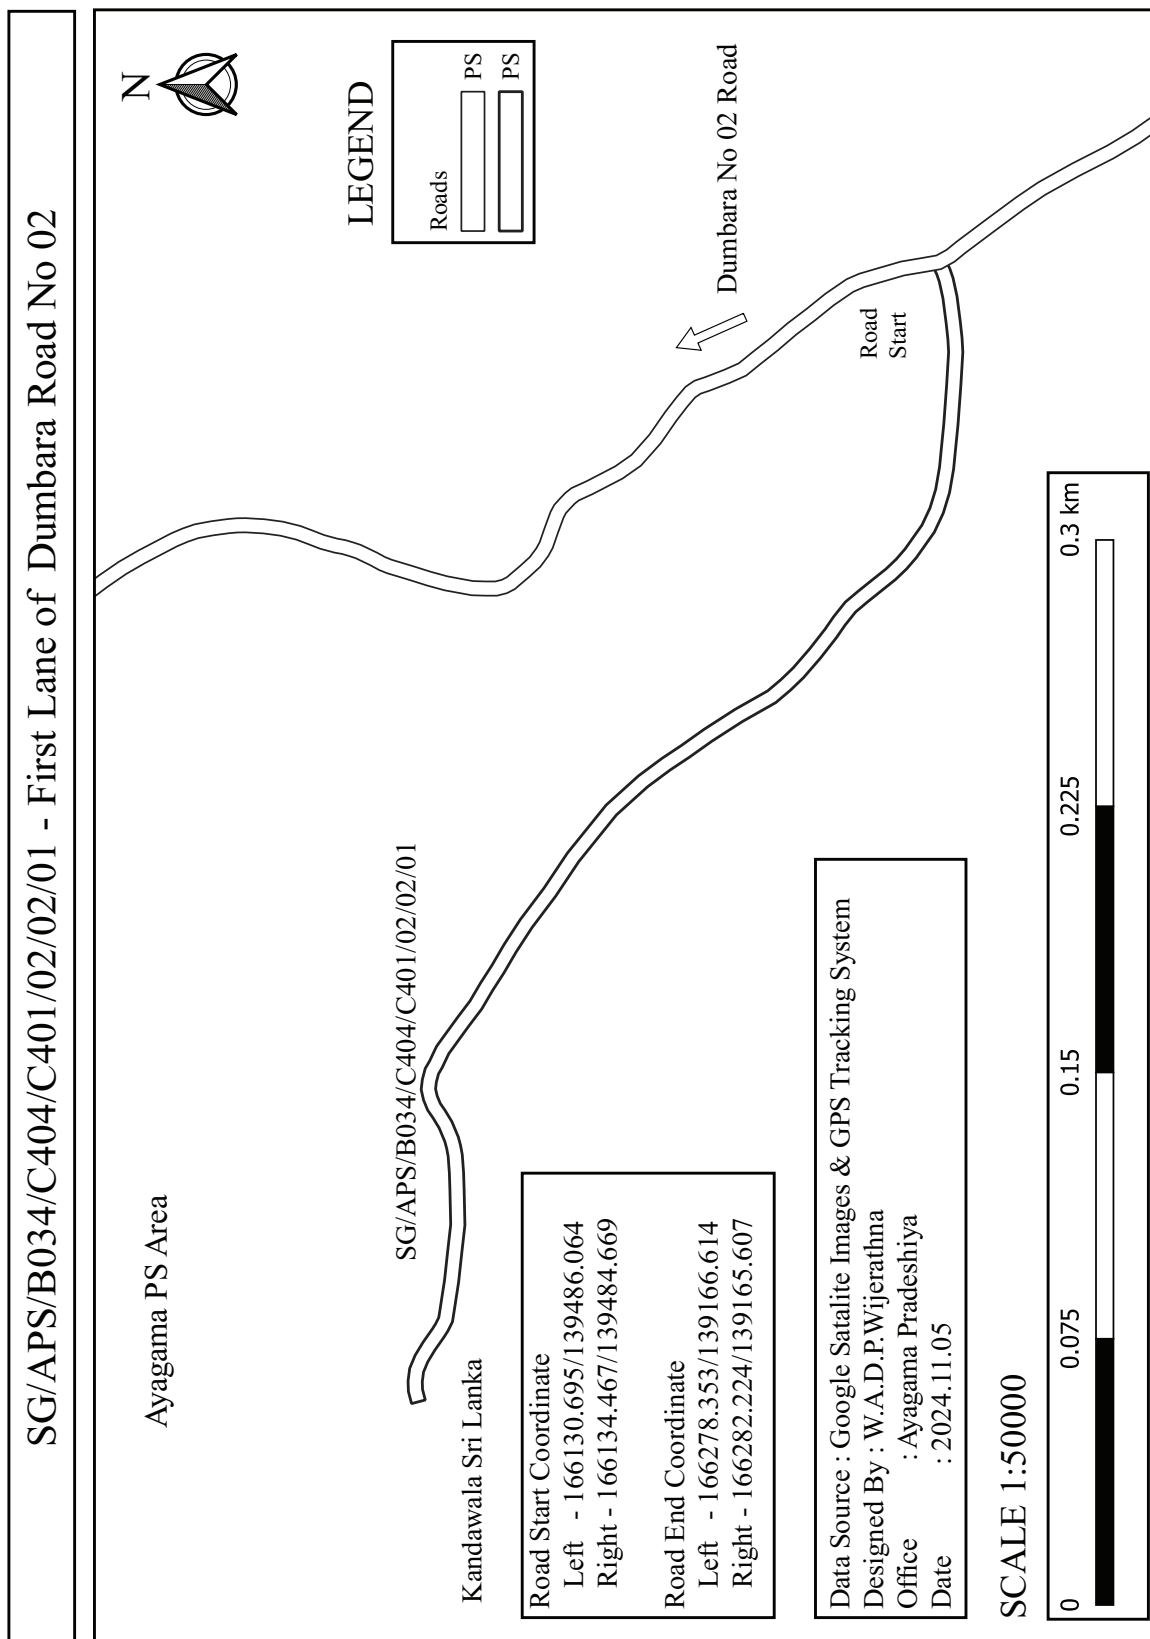

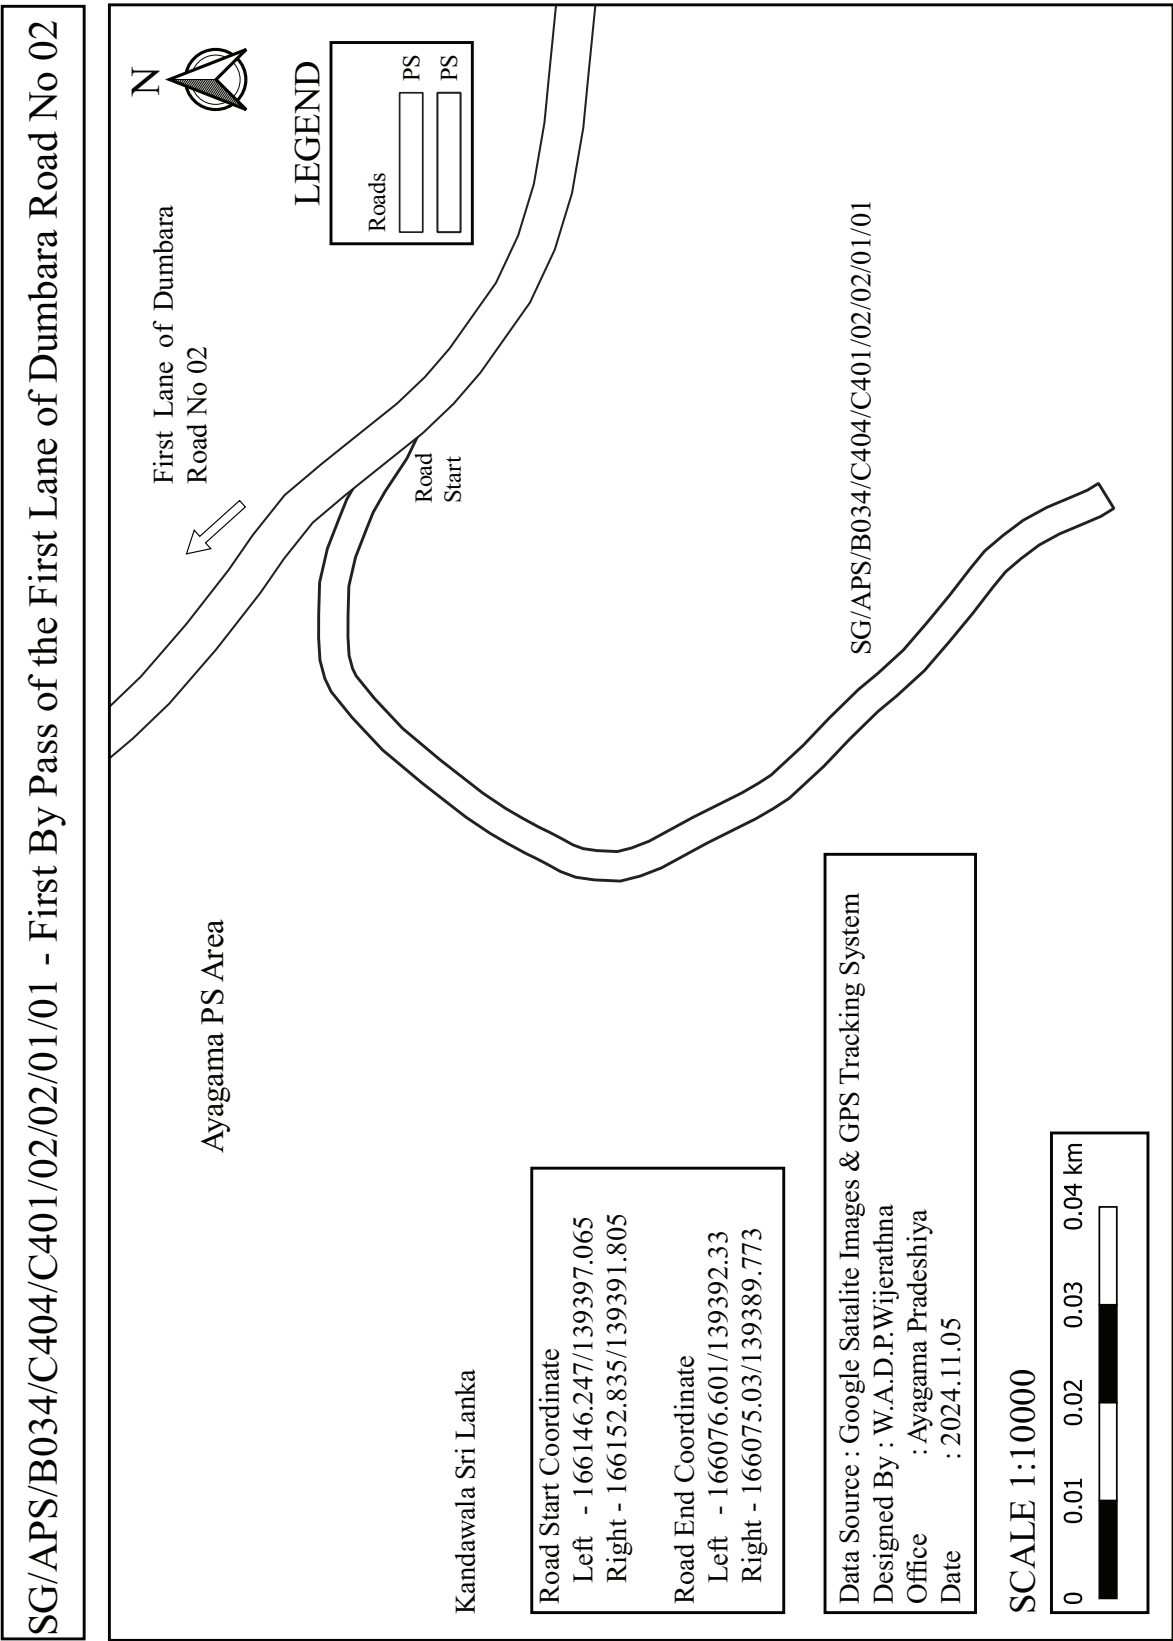


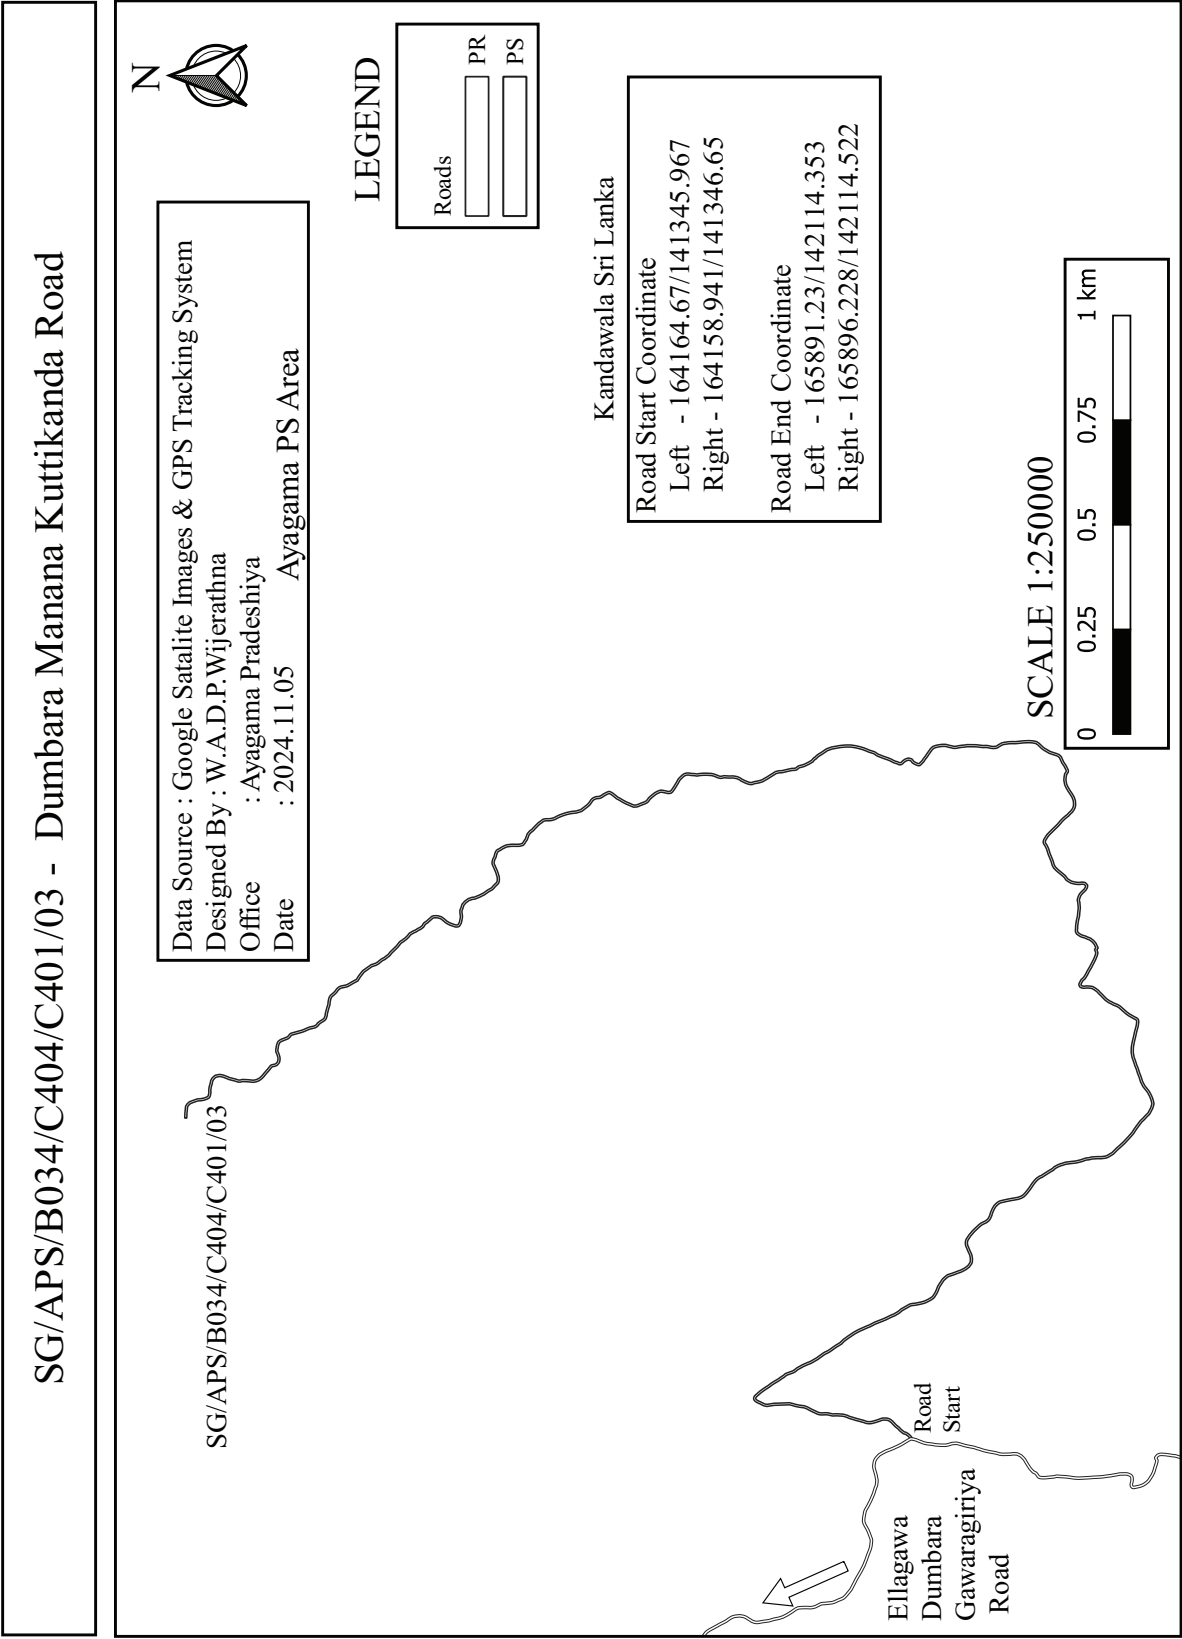


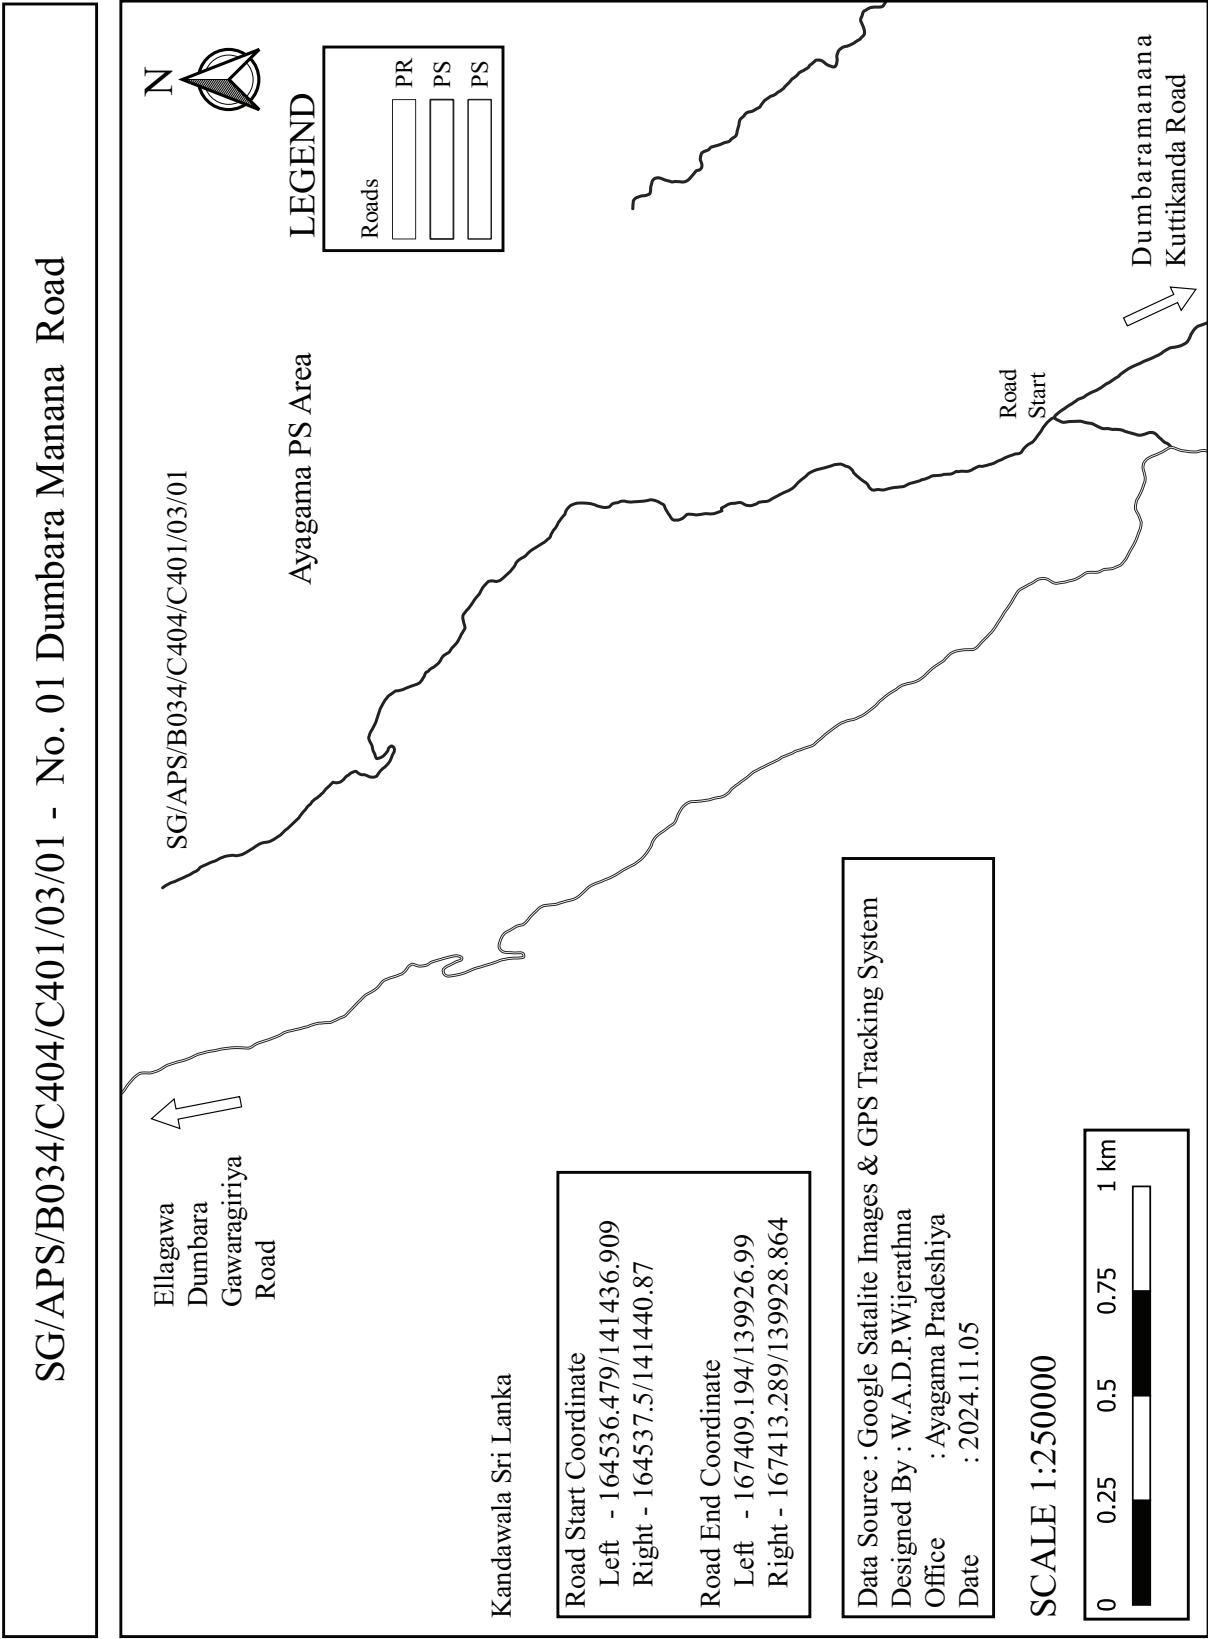

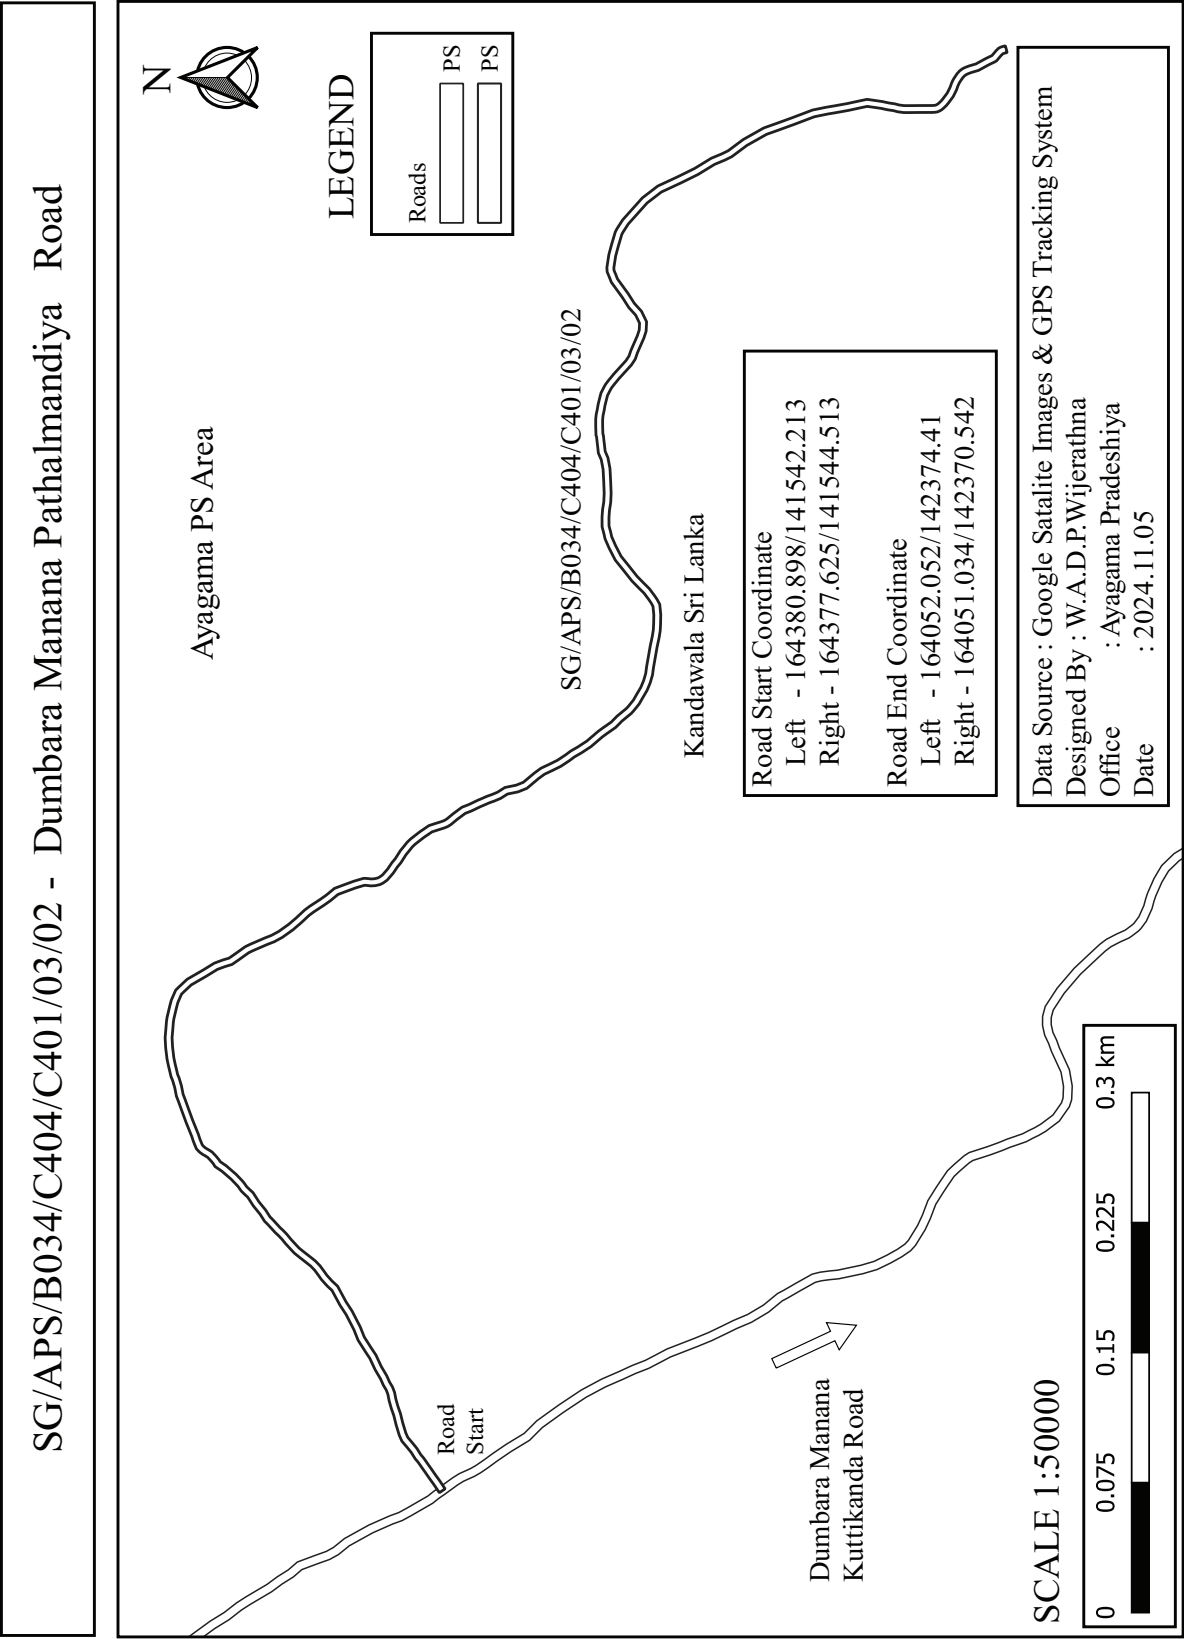





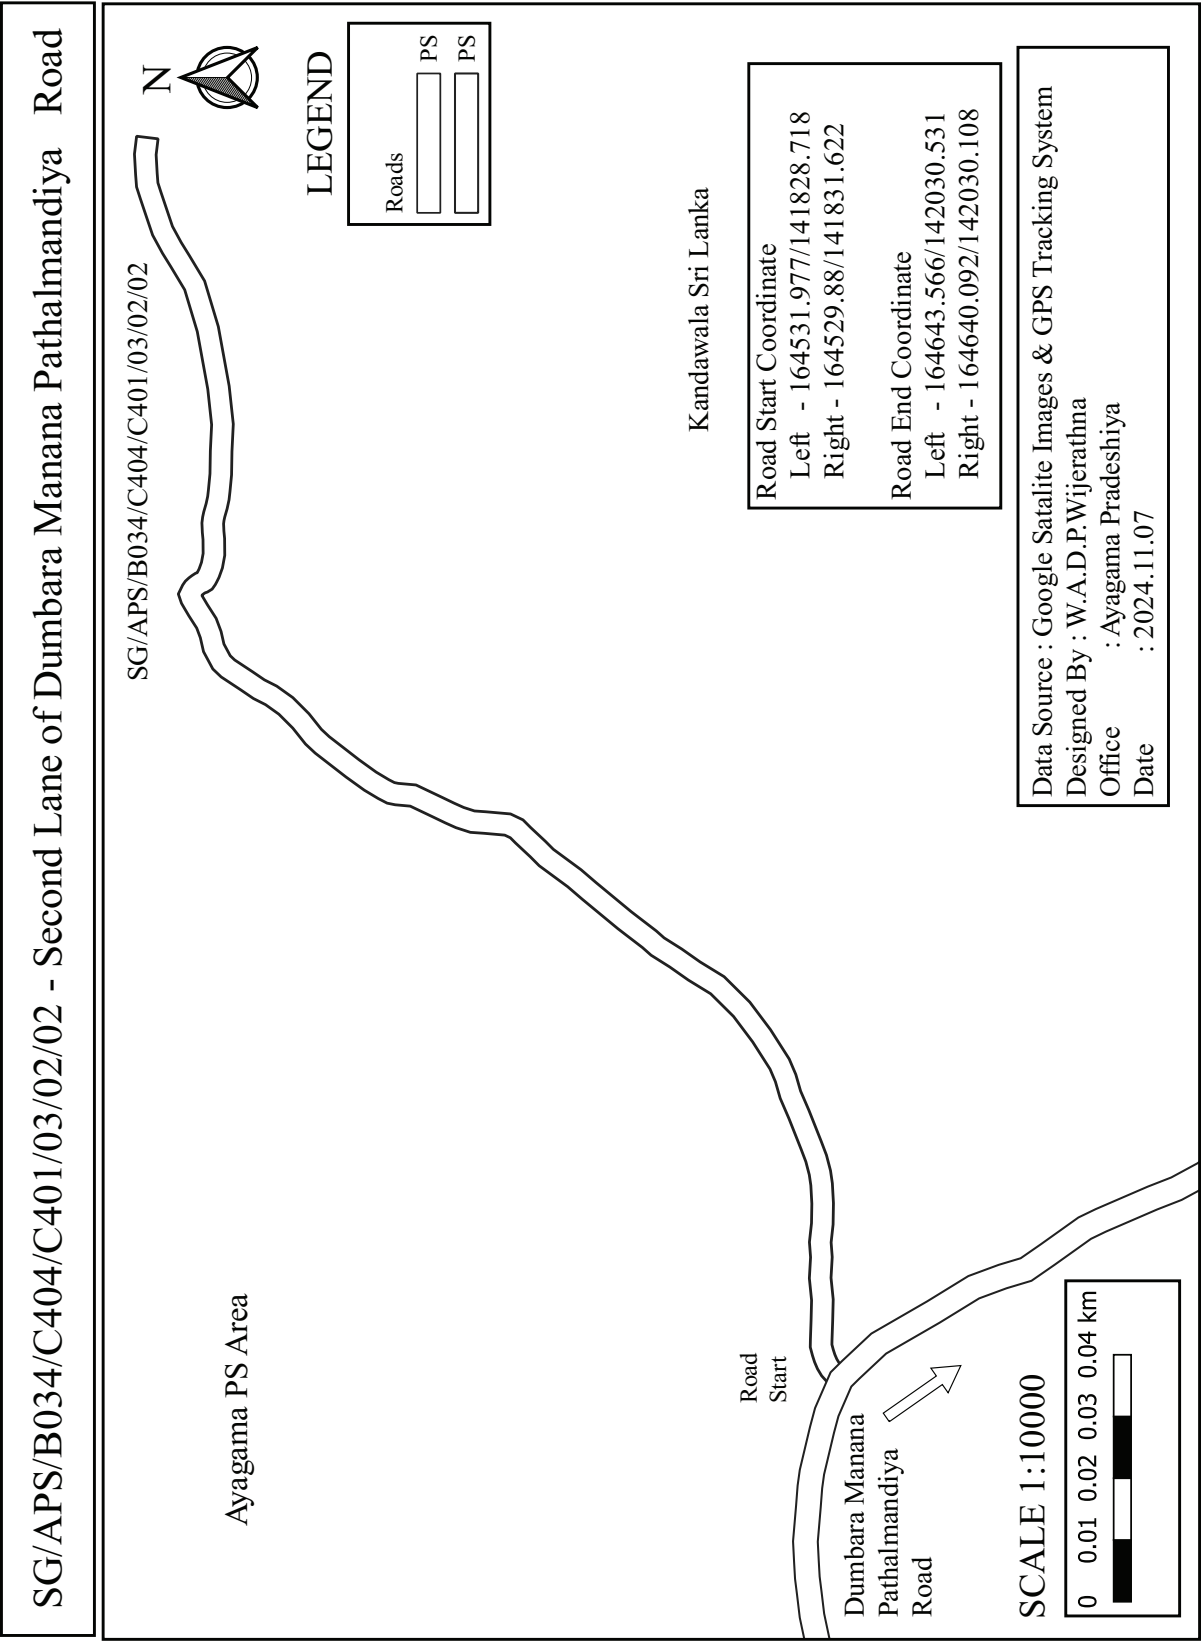


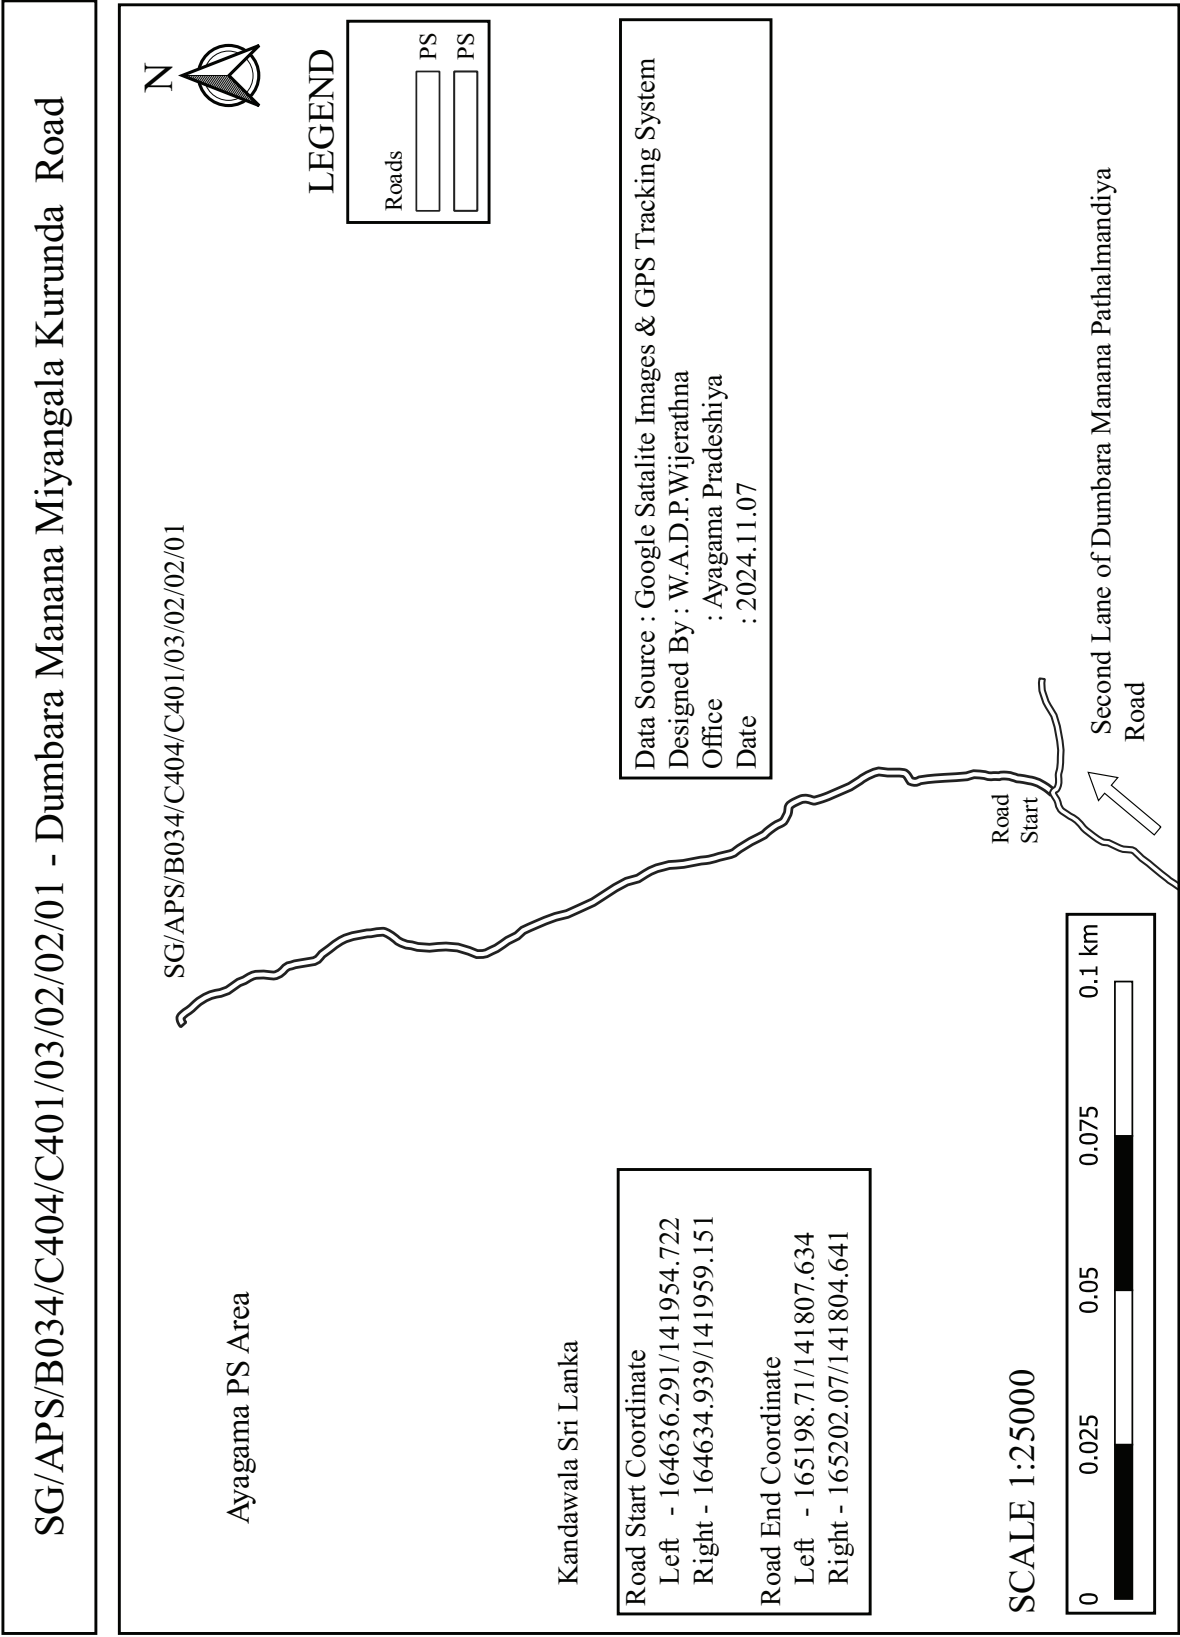





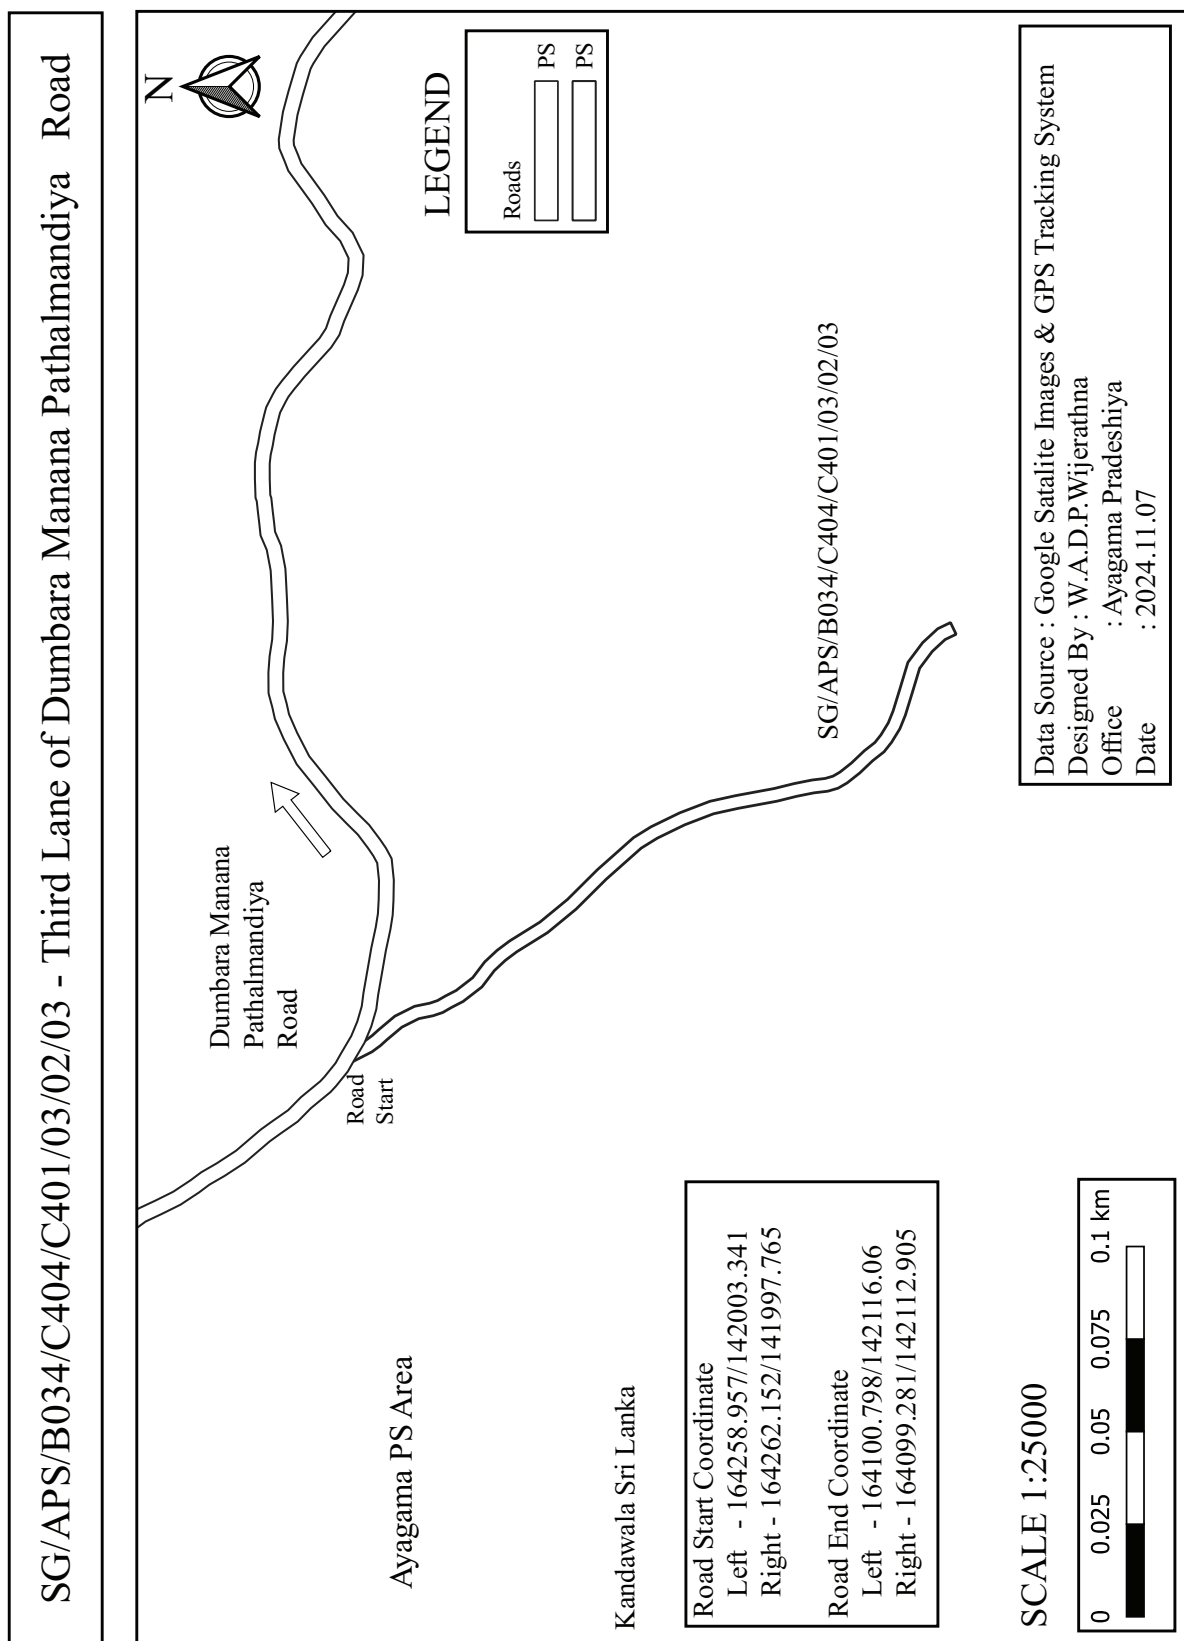


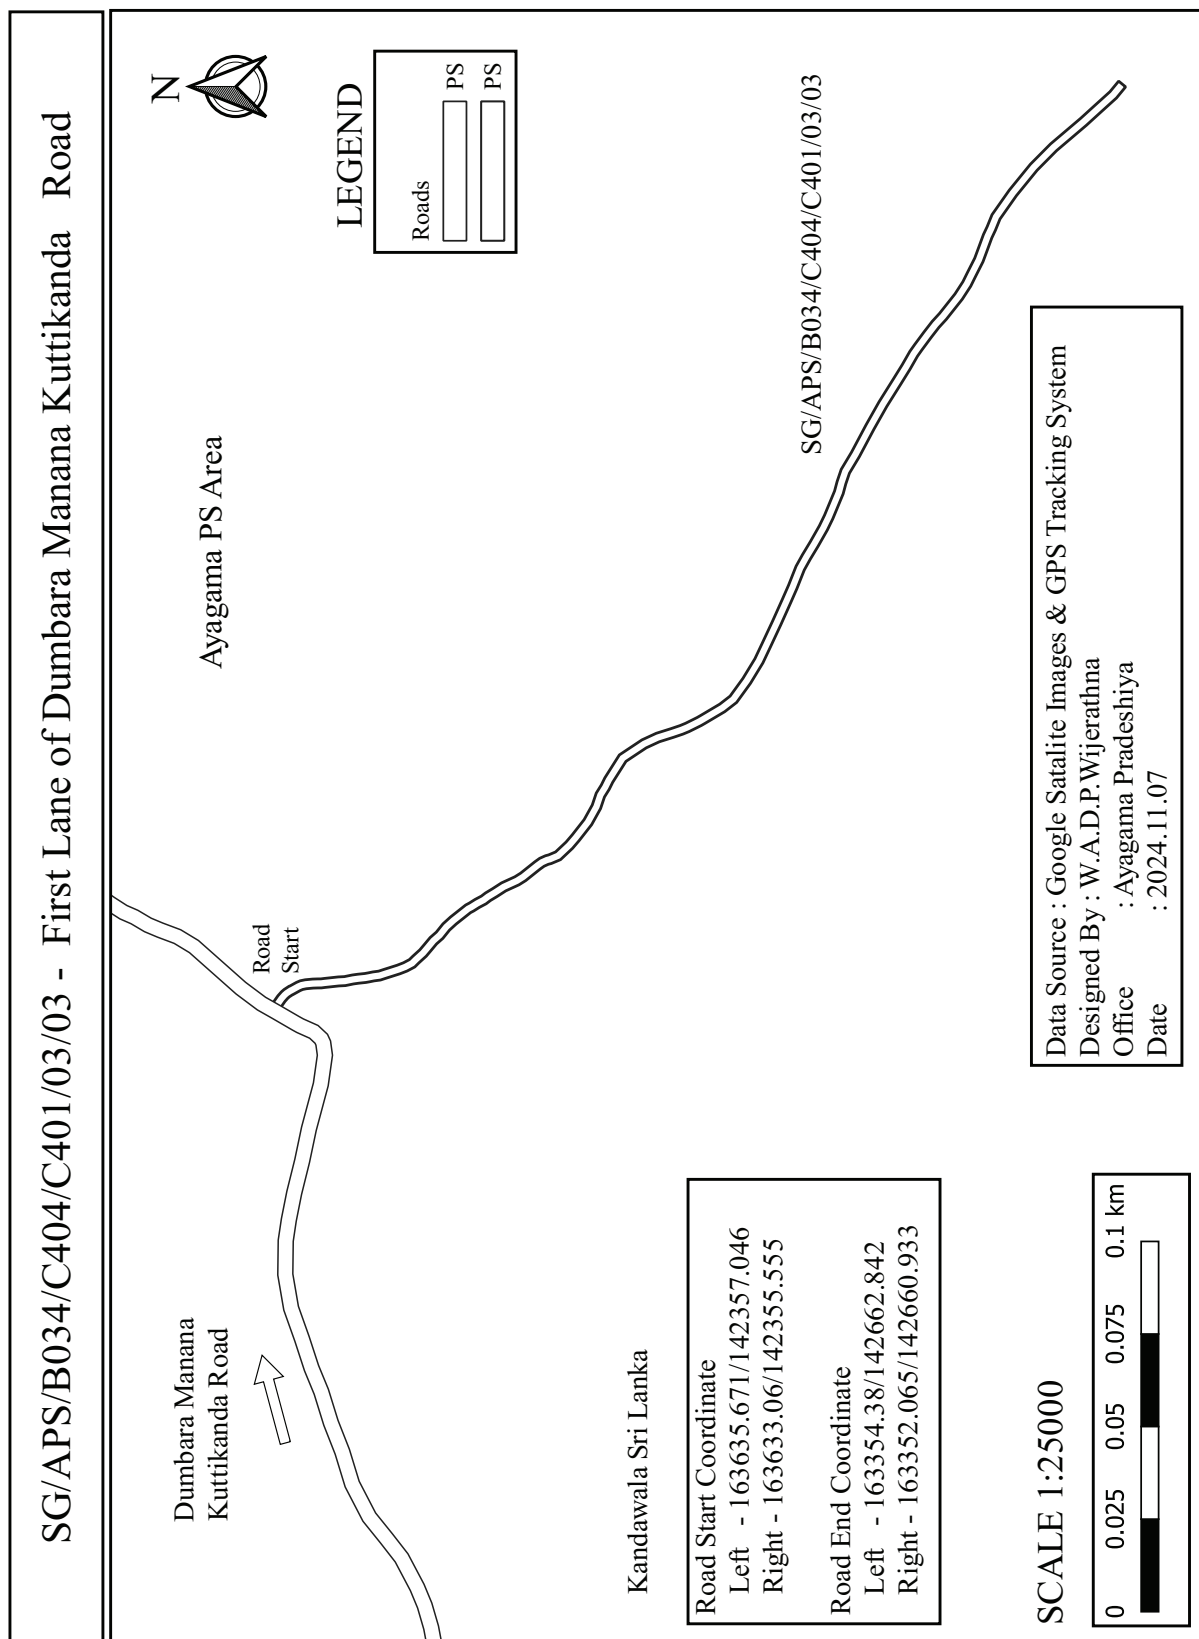


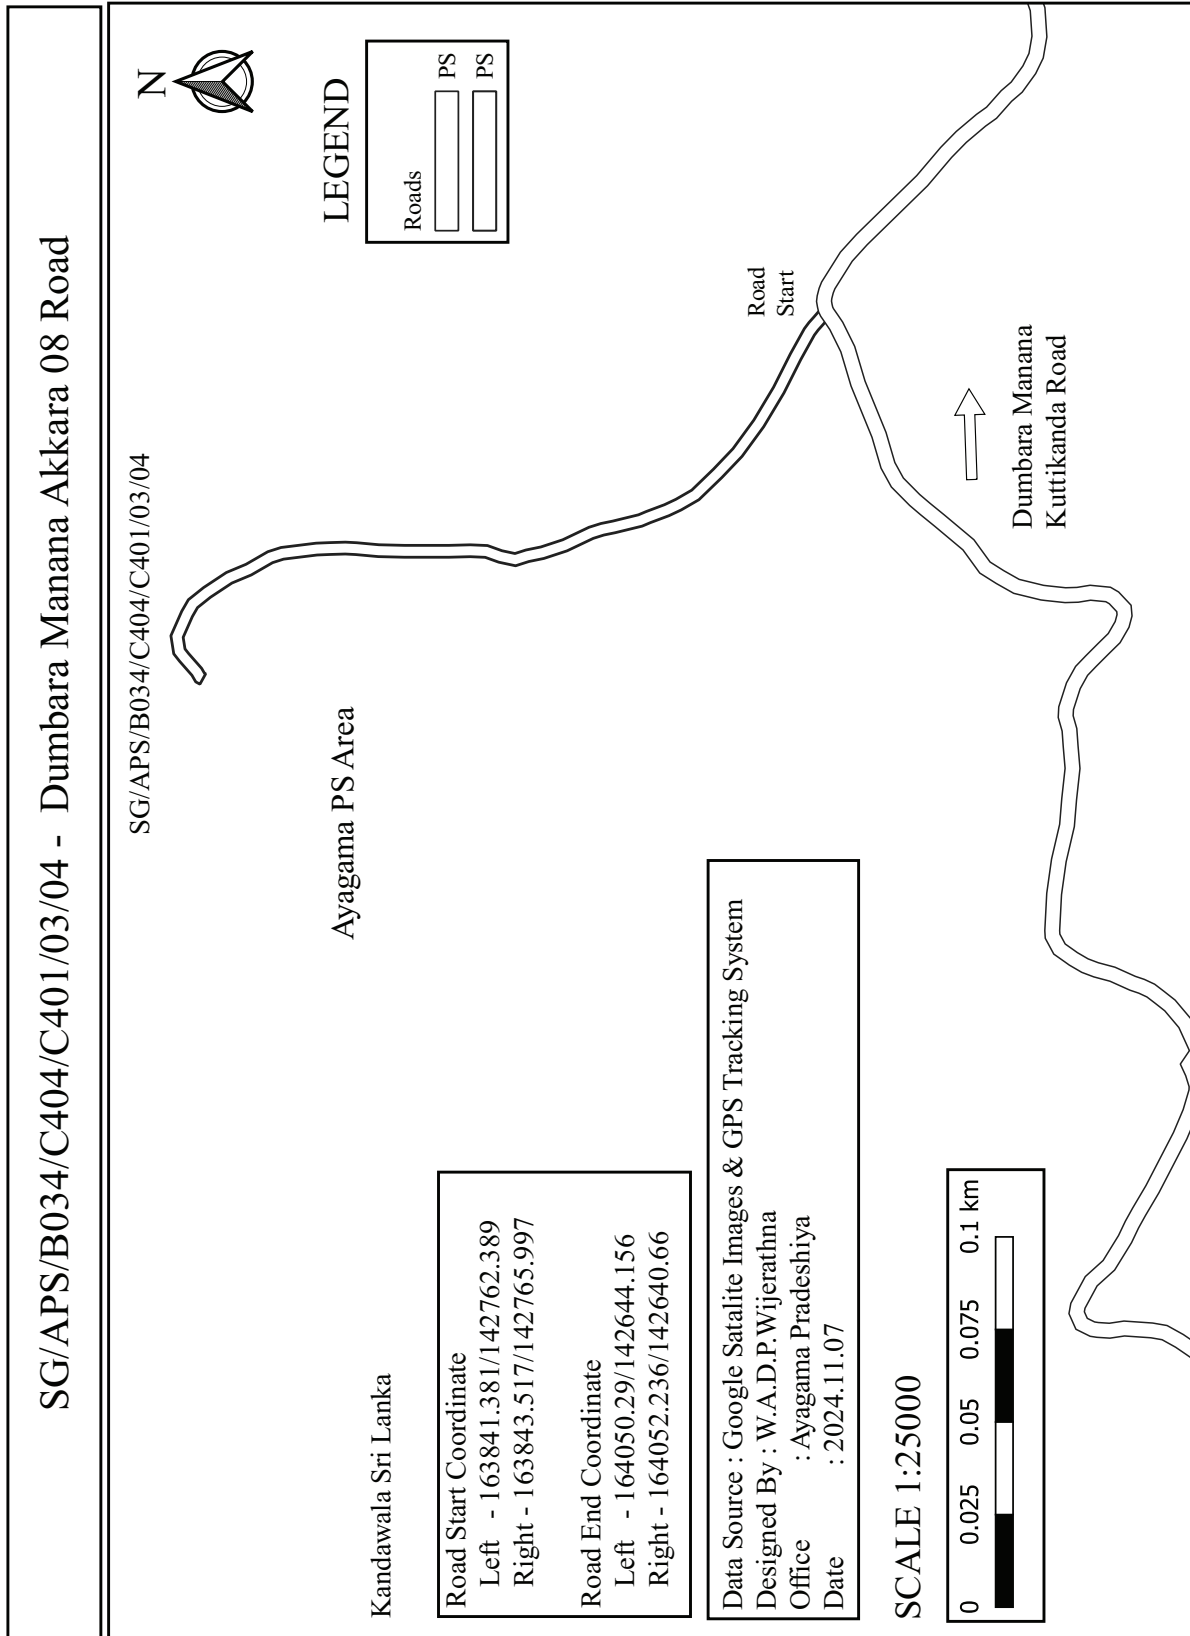

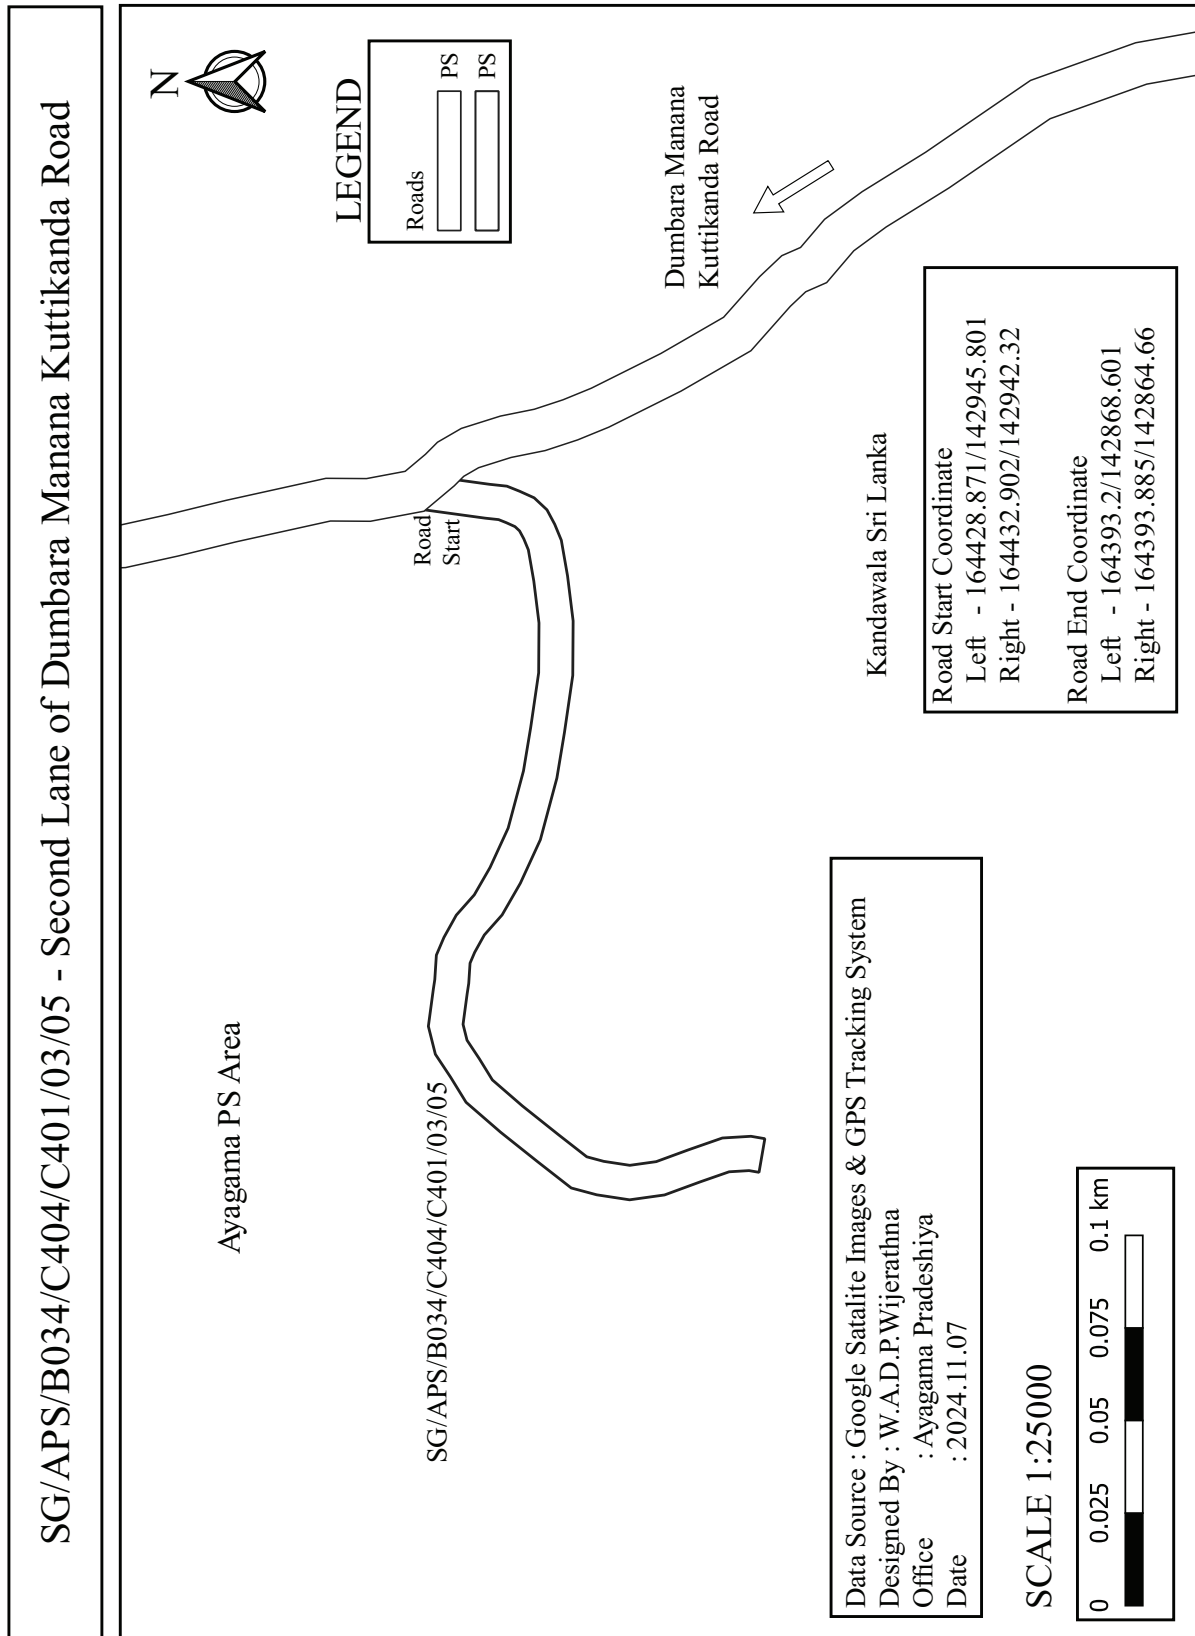

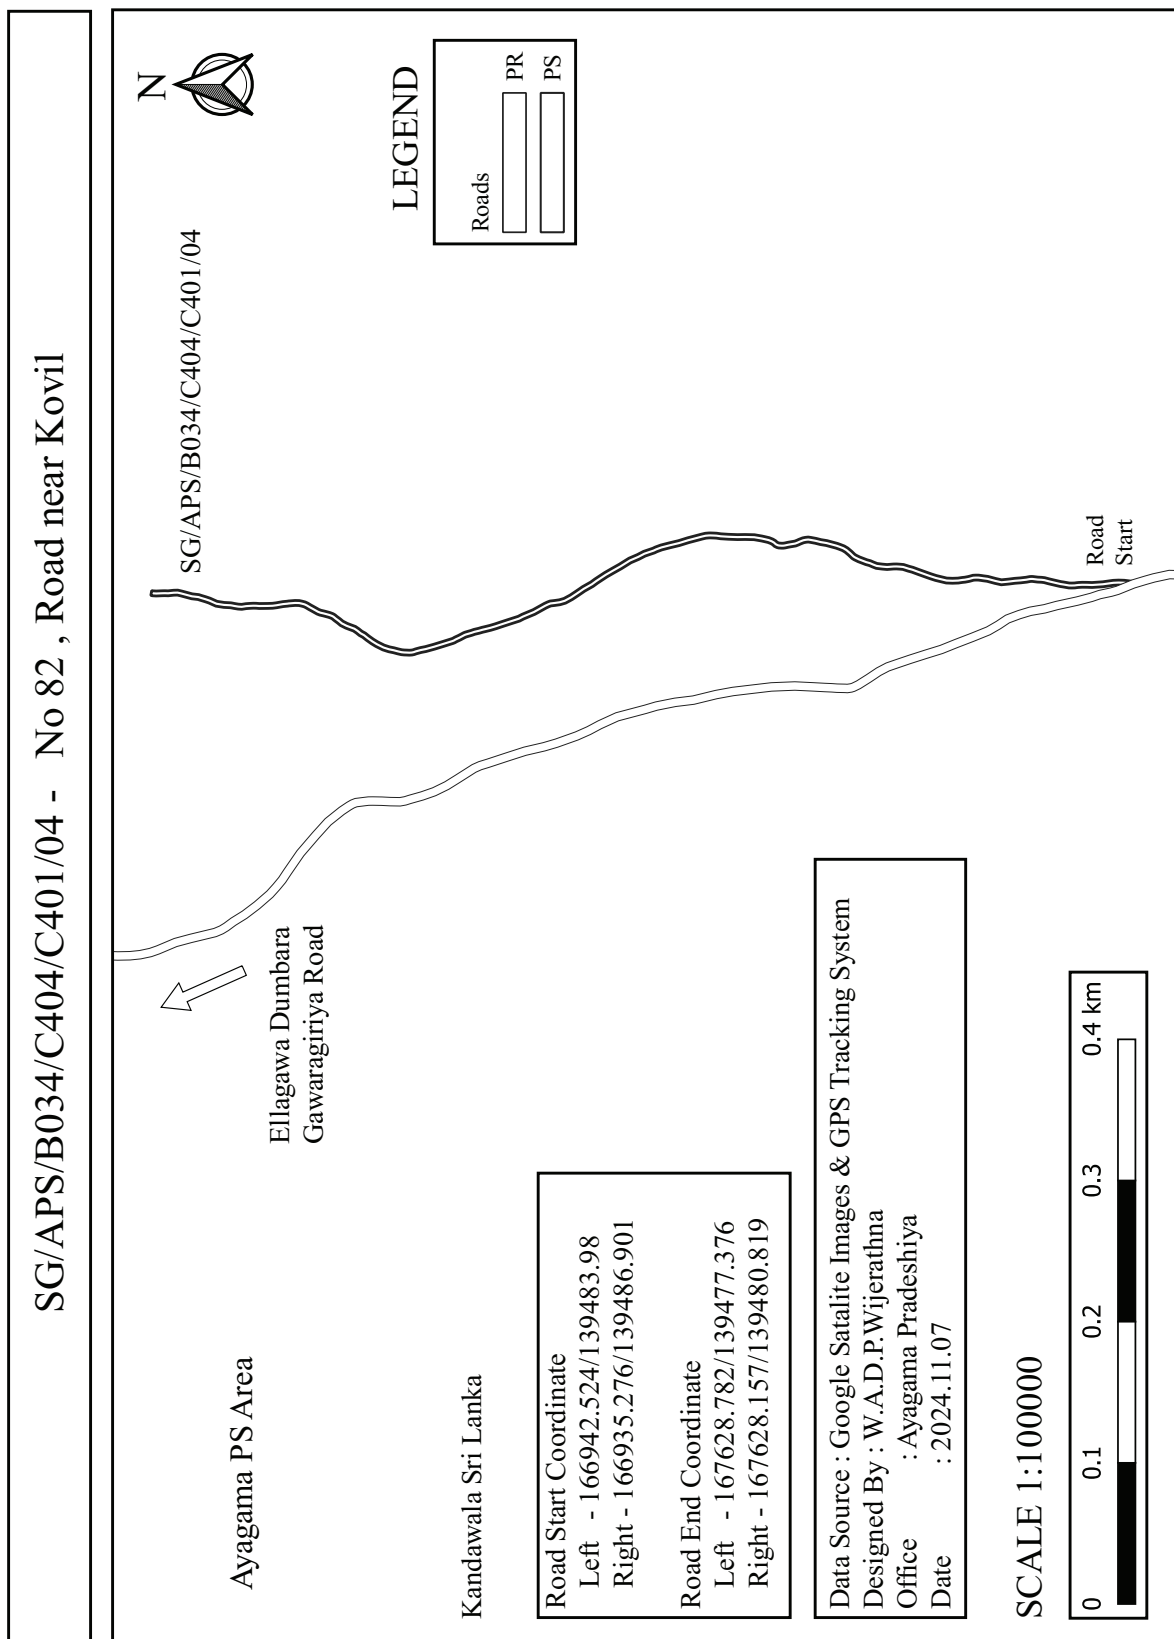

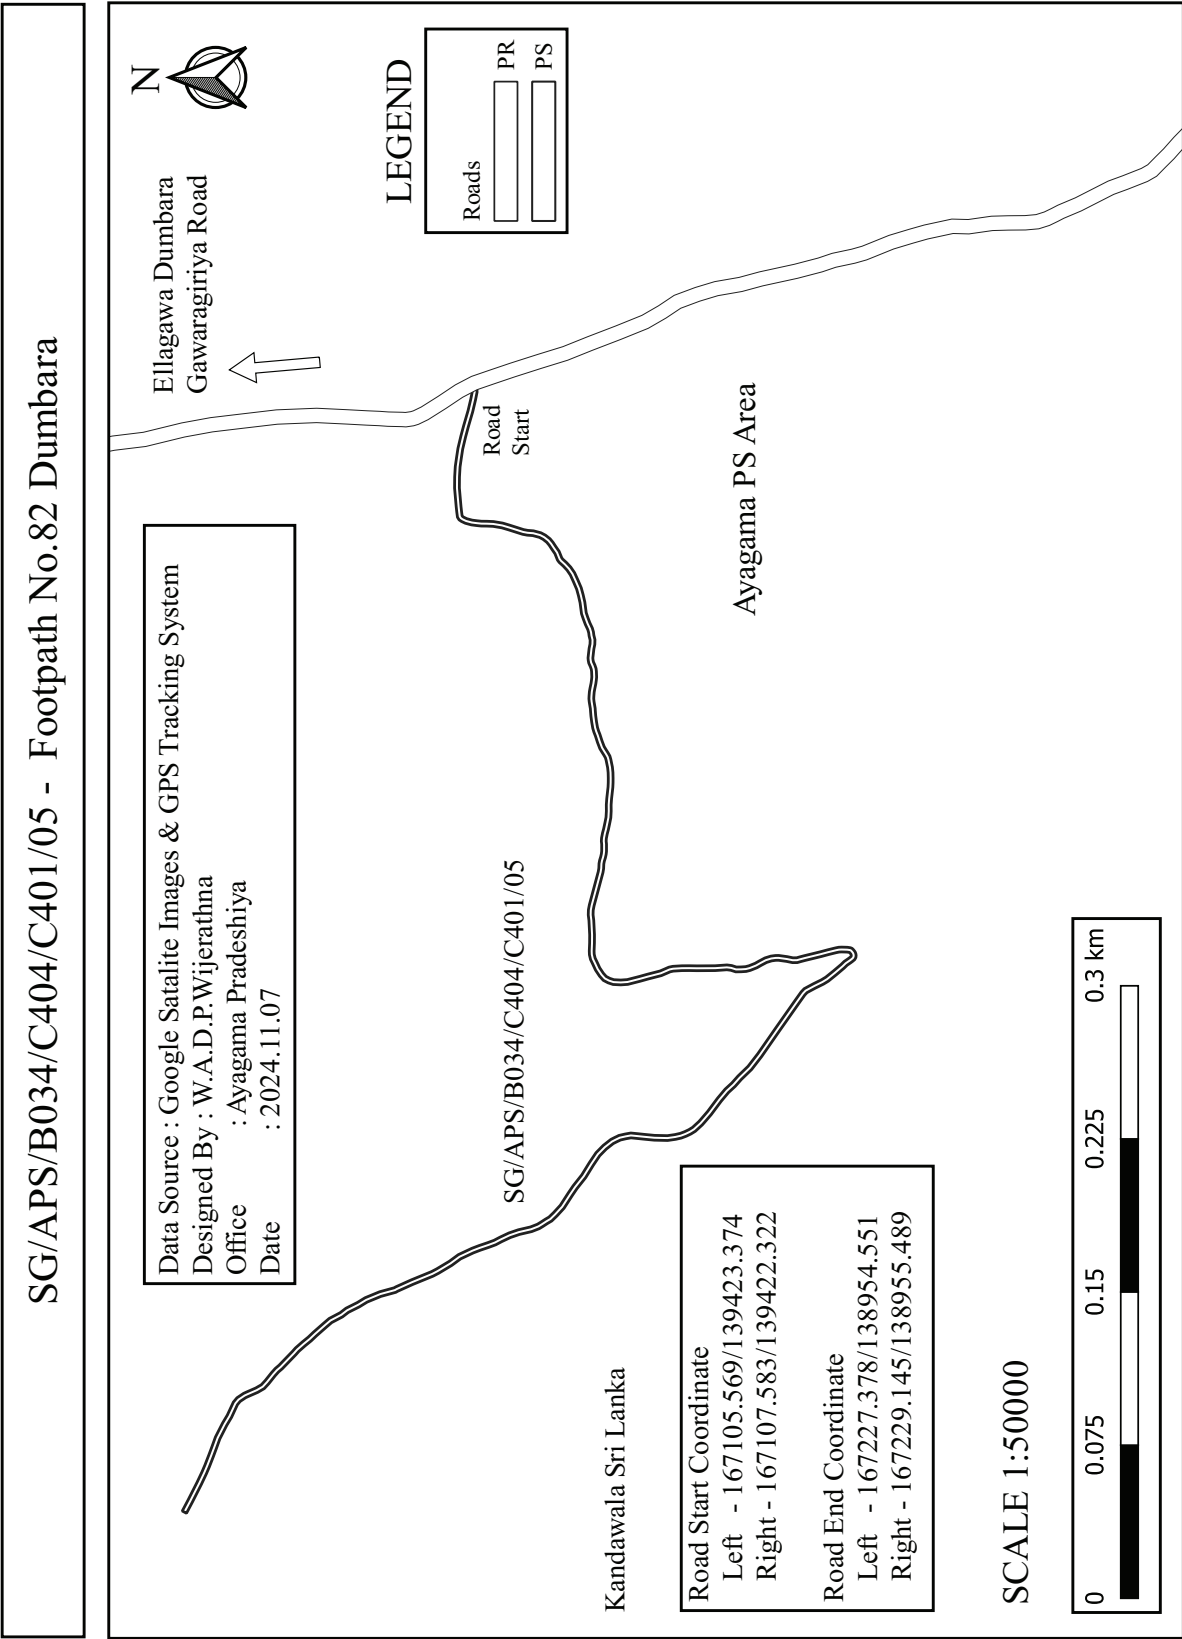

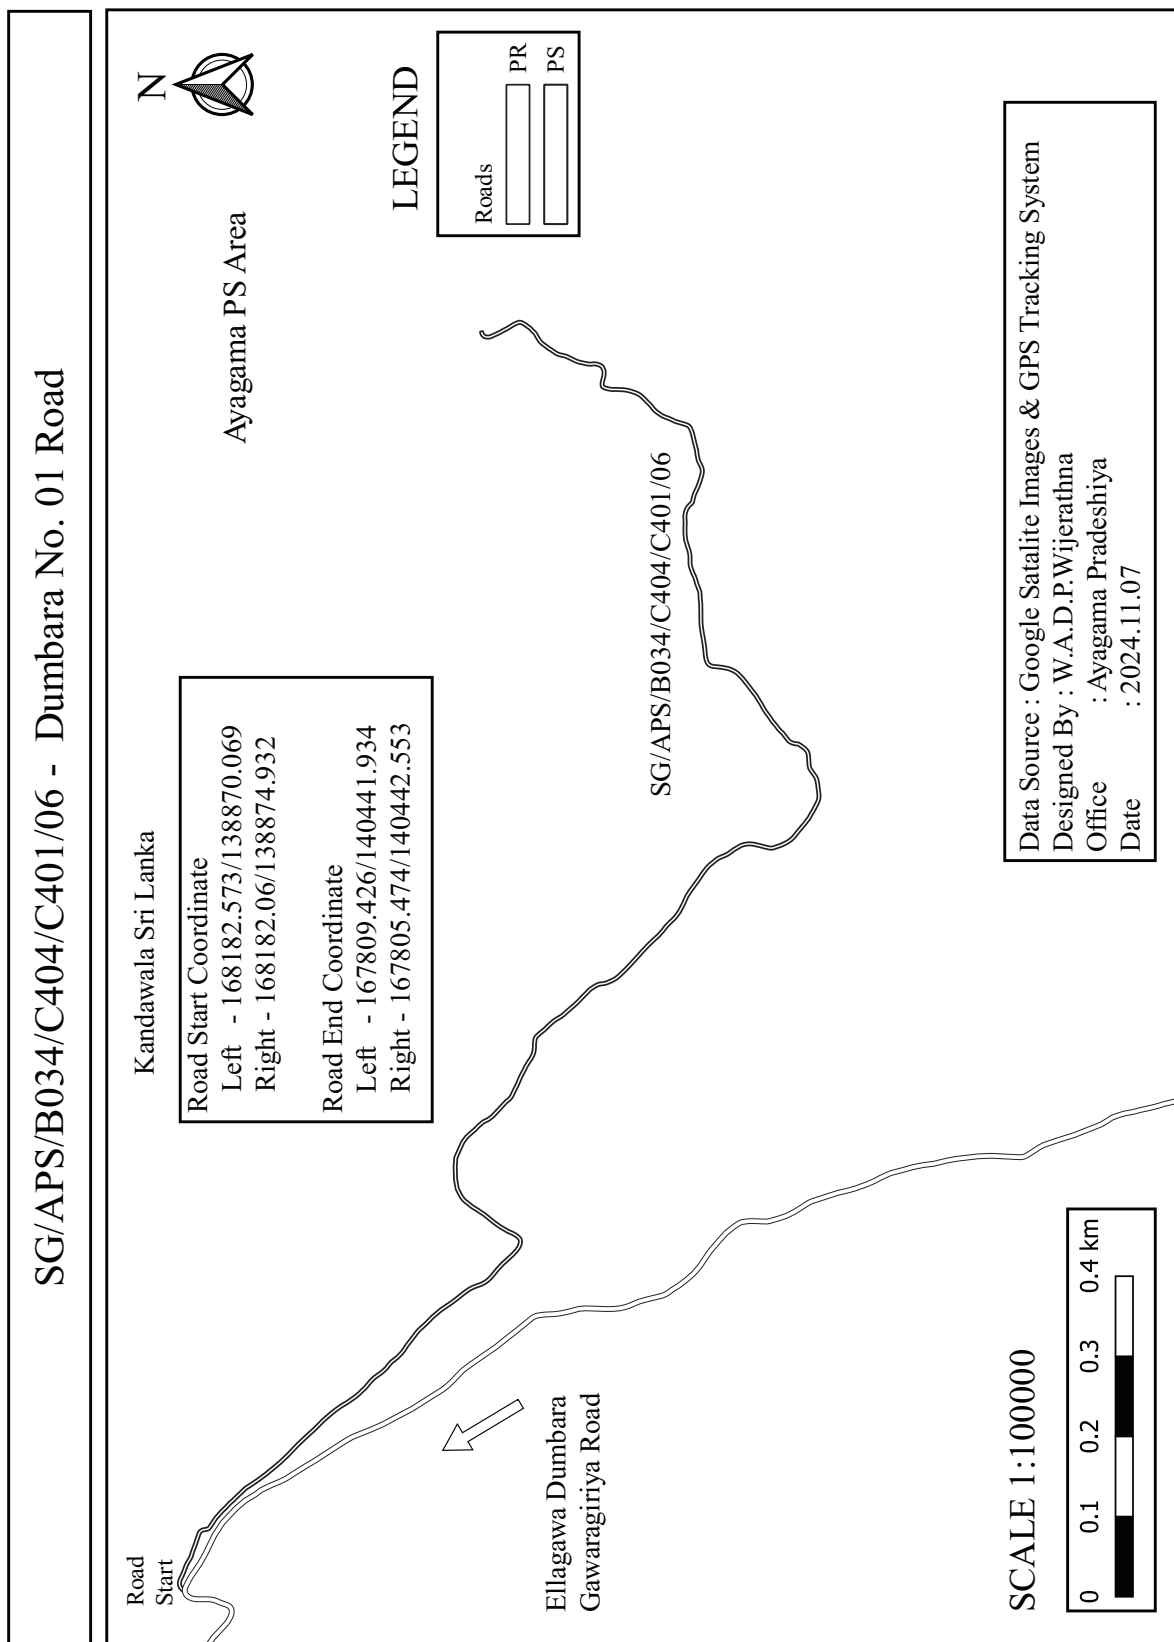

## Ayagama PS Area

SG/APS/B034/C404/C401/07

Kandawala Sri Lanka

## LEGEND

## Roads

PR

Road Start Coordinate

Left - 168219.125/138592.16

Right - 168214.867/138602.546

Road End Coordinate

Left - 168972.466/138633.193

Right - 168973.006/138637.156

**Data Source : Google Satalite Images & GPS Tracking System**

Designed By : W.A.D.P.Wijerathna

Office : Ayagama Pradeshiya

Date : 2024.11.07


SCALE 1:100000


| 0 | 0.1 | 0.2 | 0.3 | 0.4 km |
|---|-----|-----|-----|--------|
|---|-----|-----|-----|--------|


Ellagawa Dumbara  
Gawaragiriya Road


Road  
Start




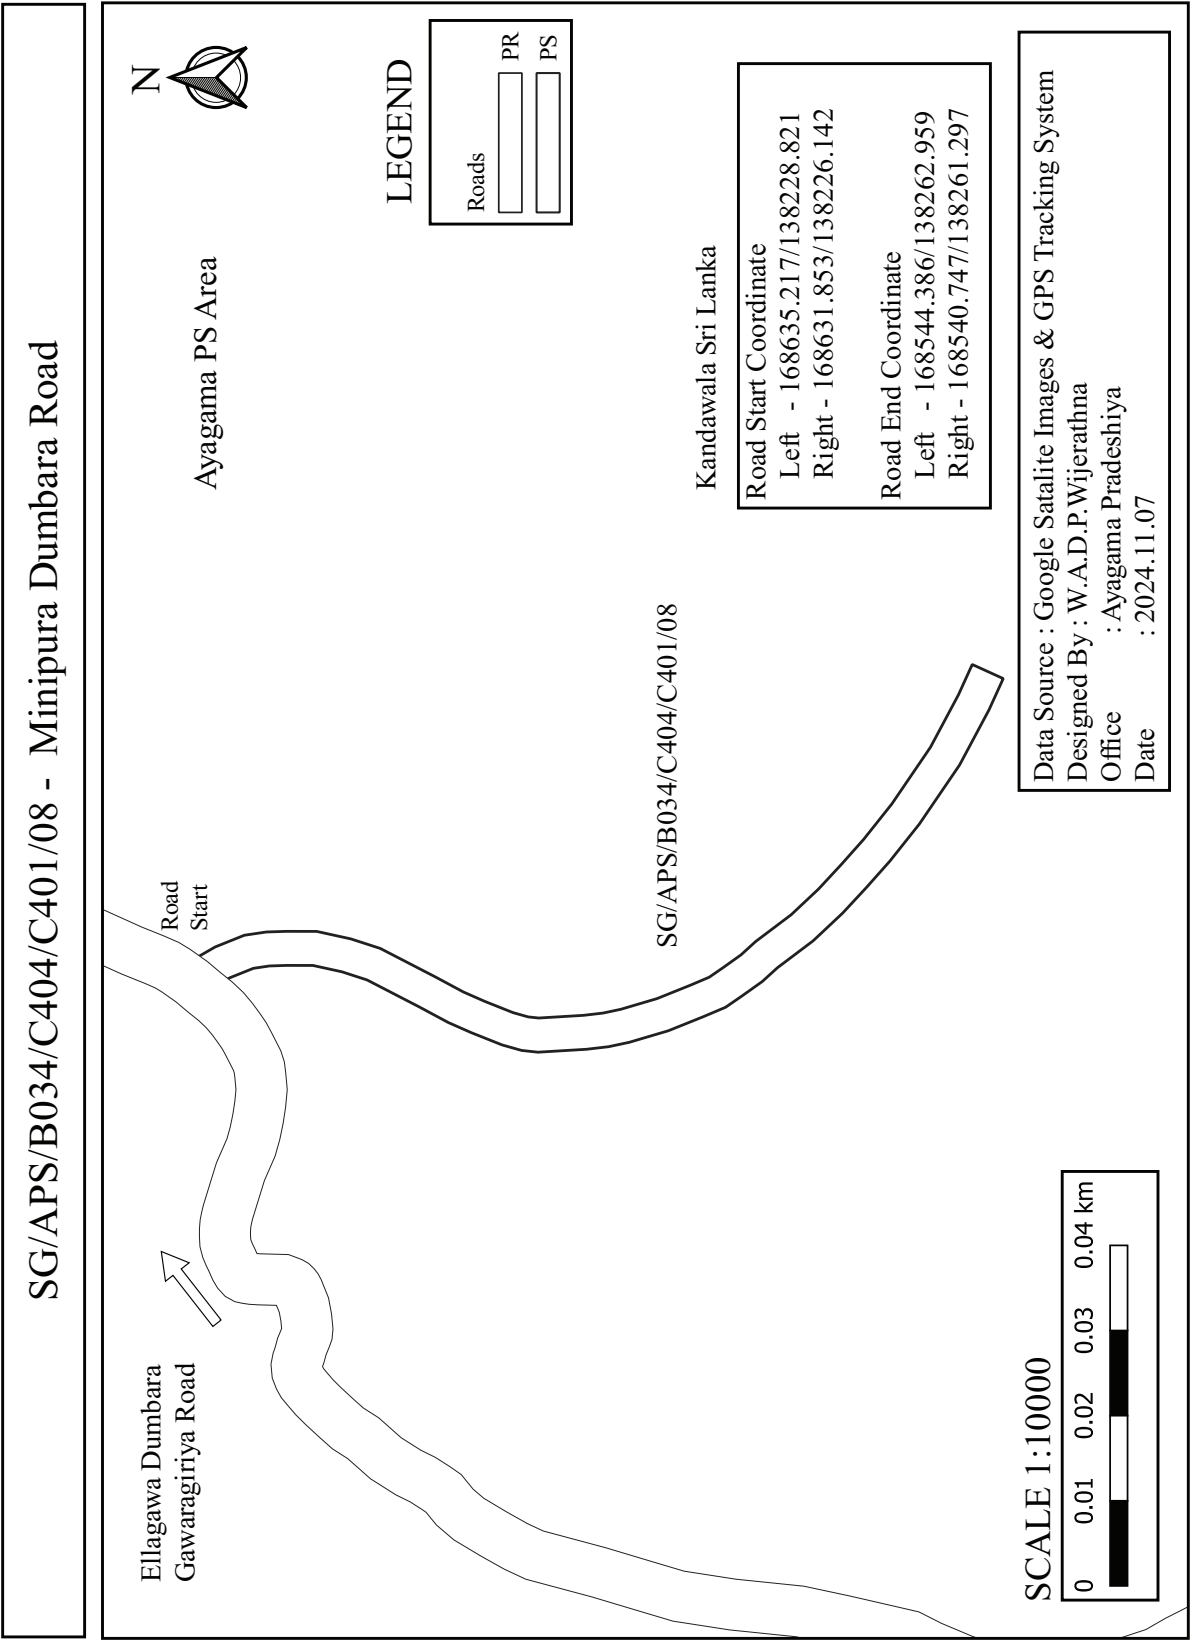


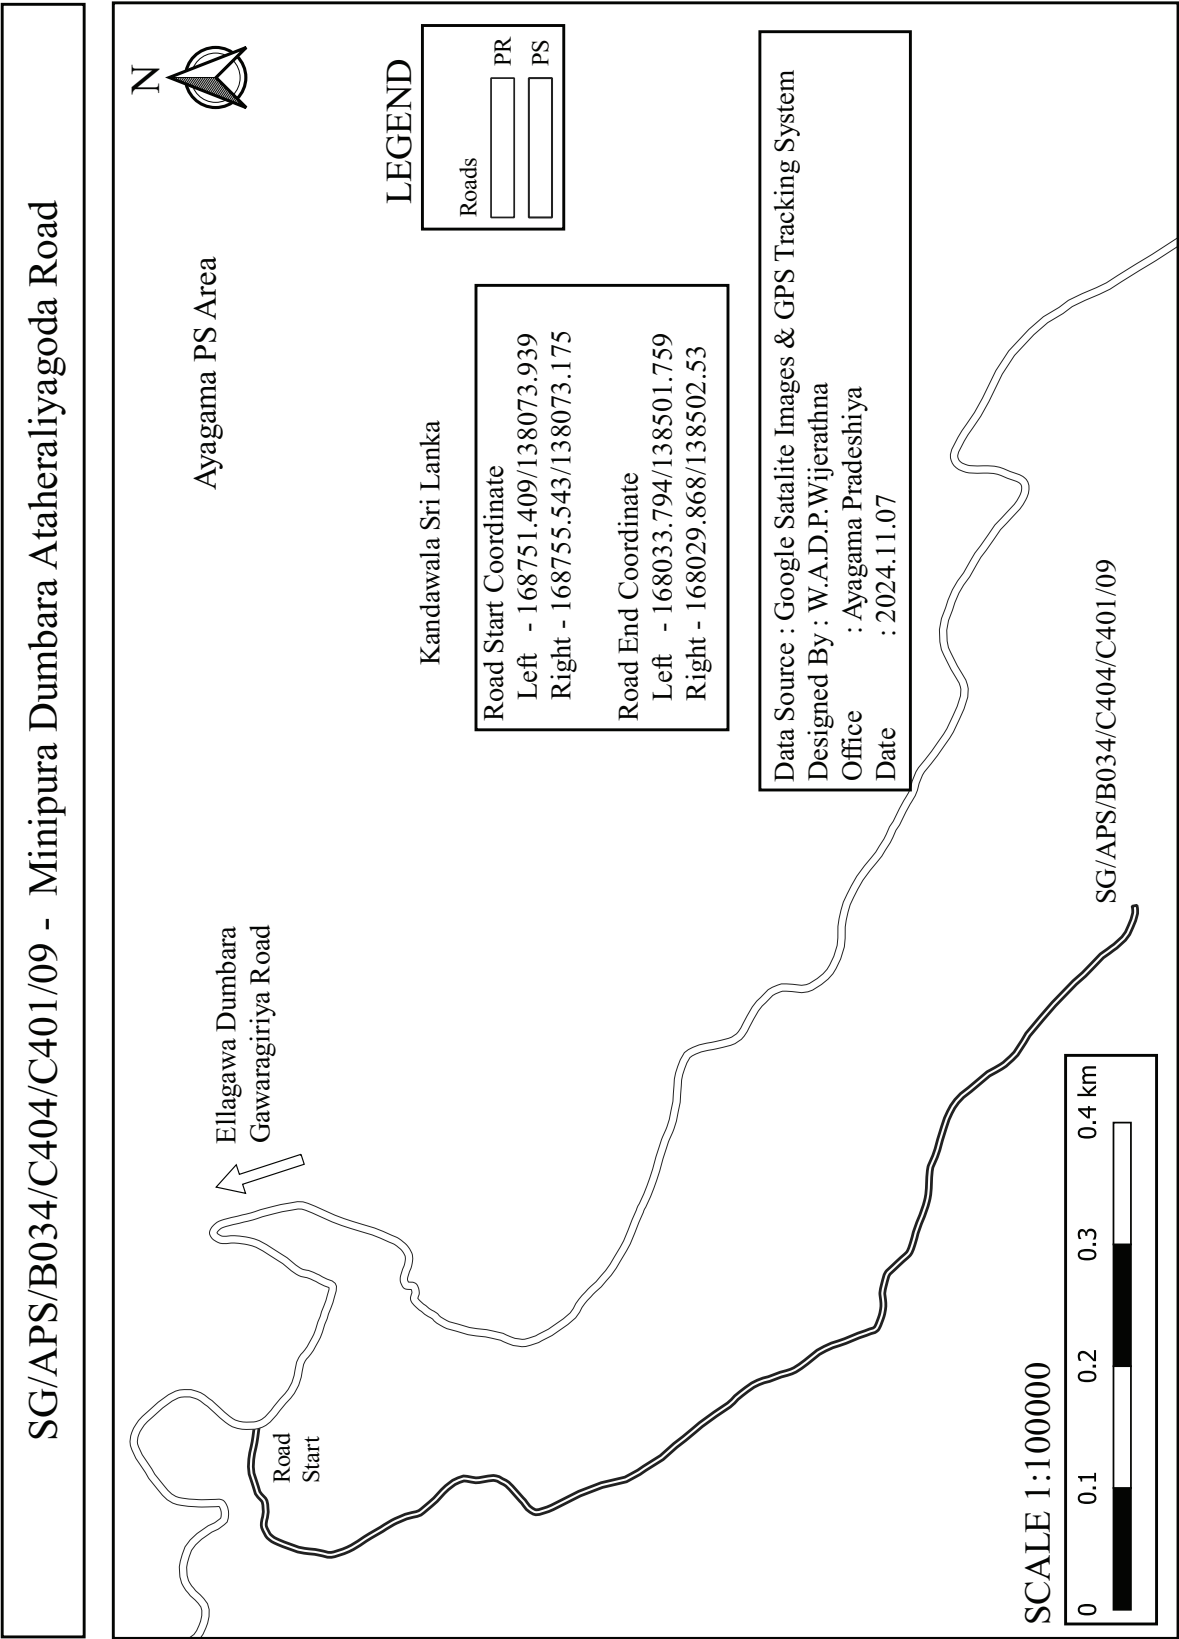


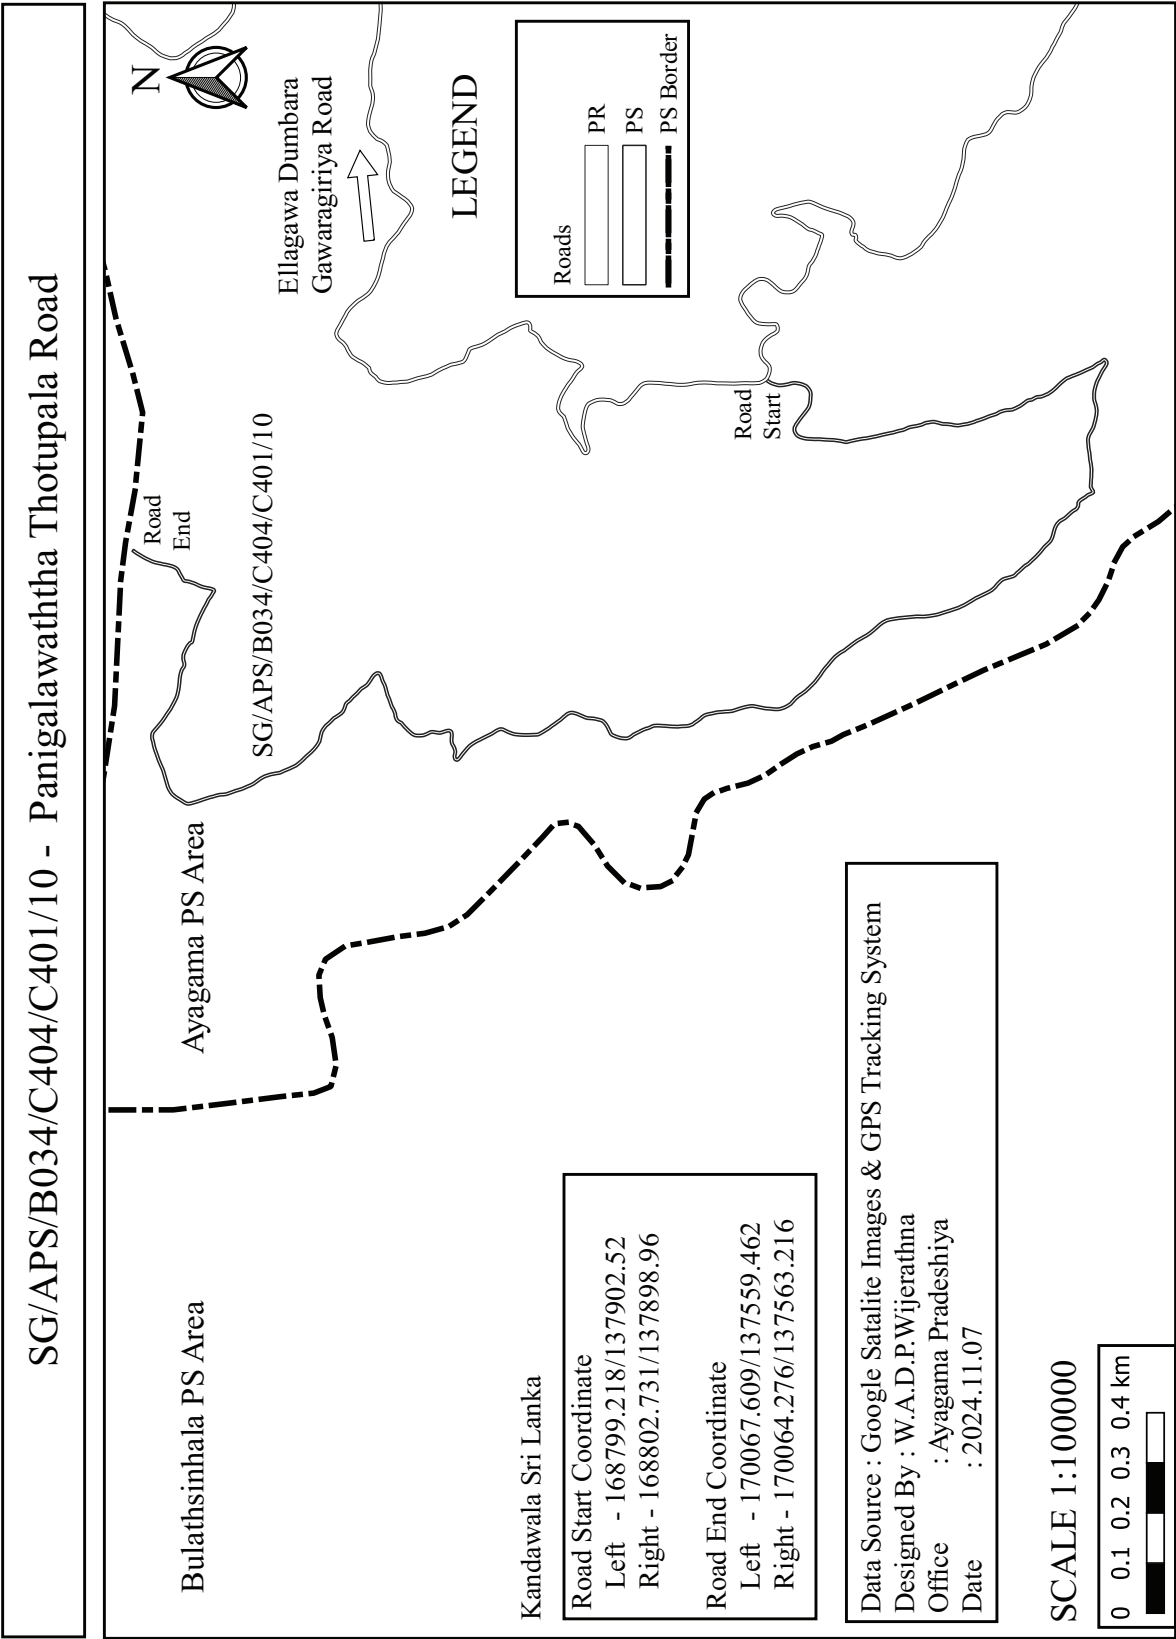


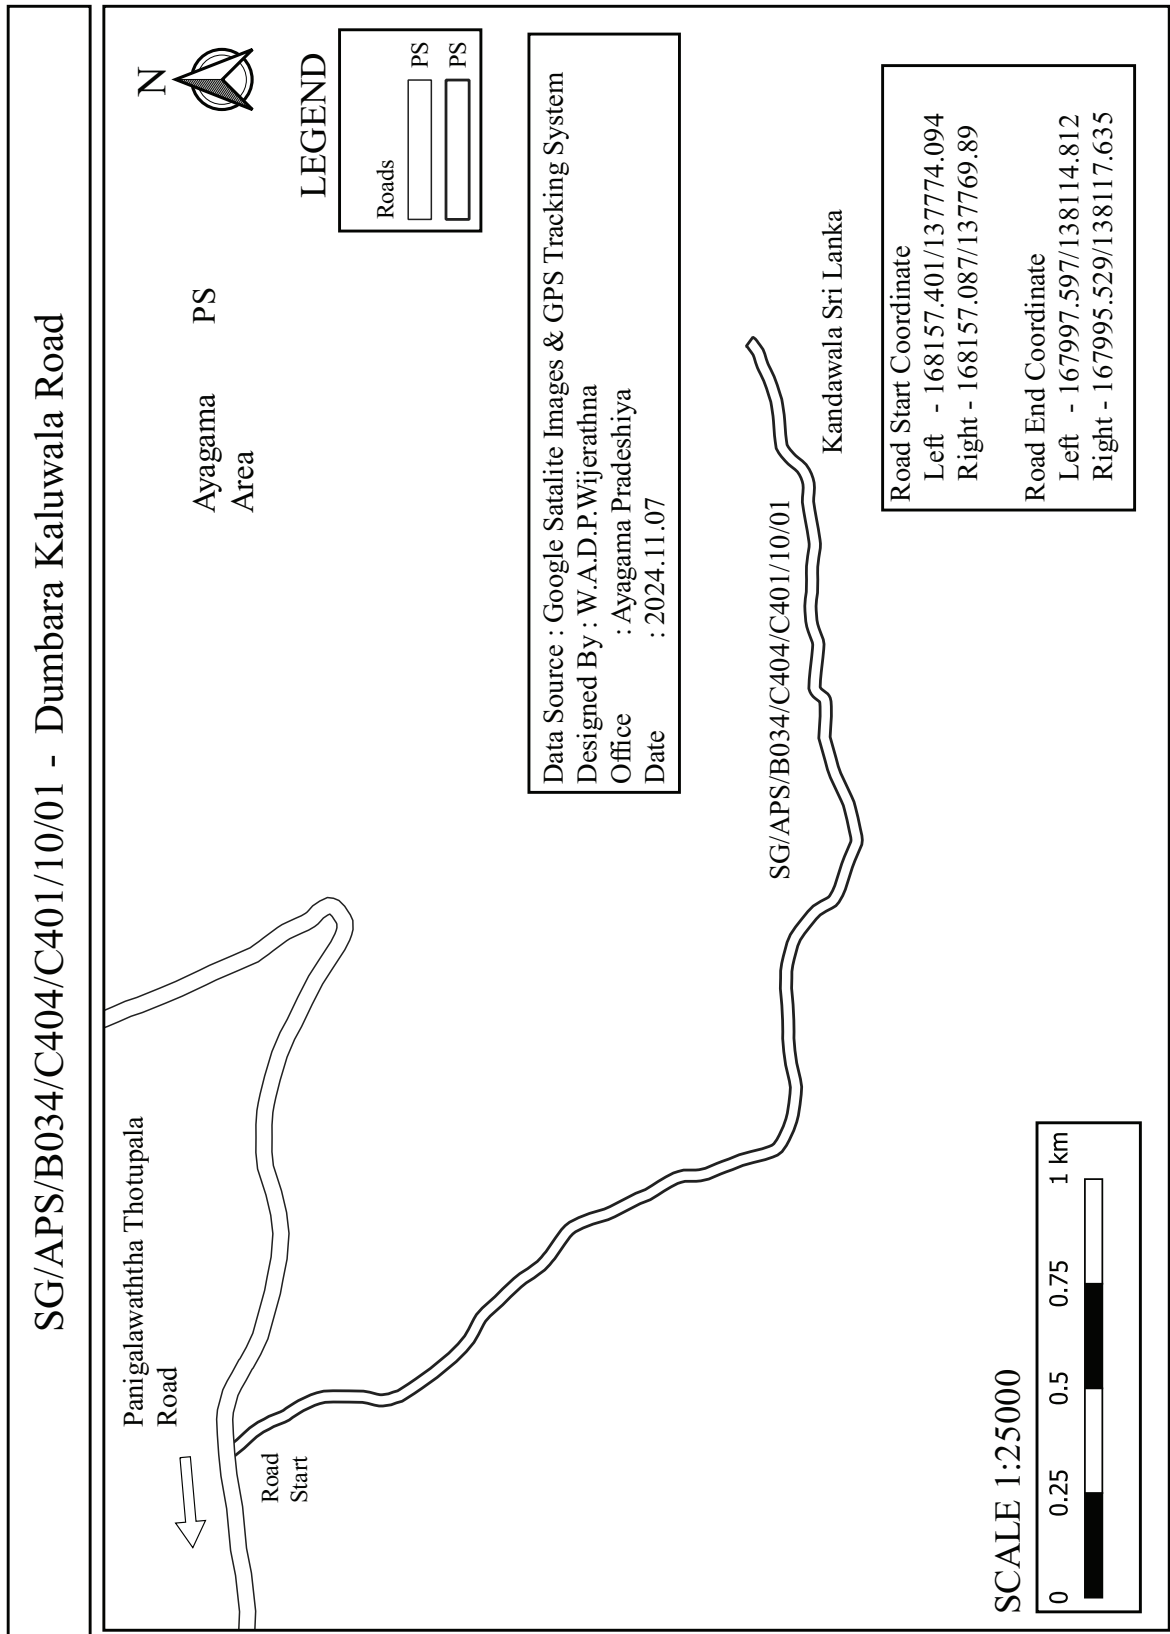

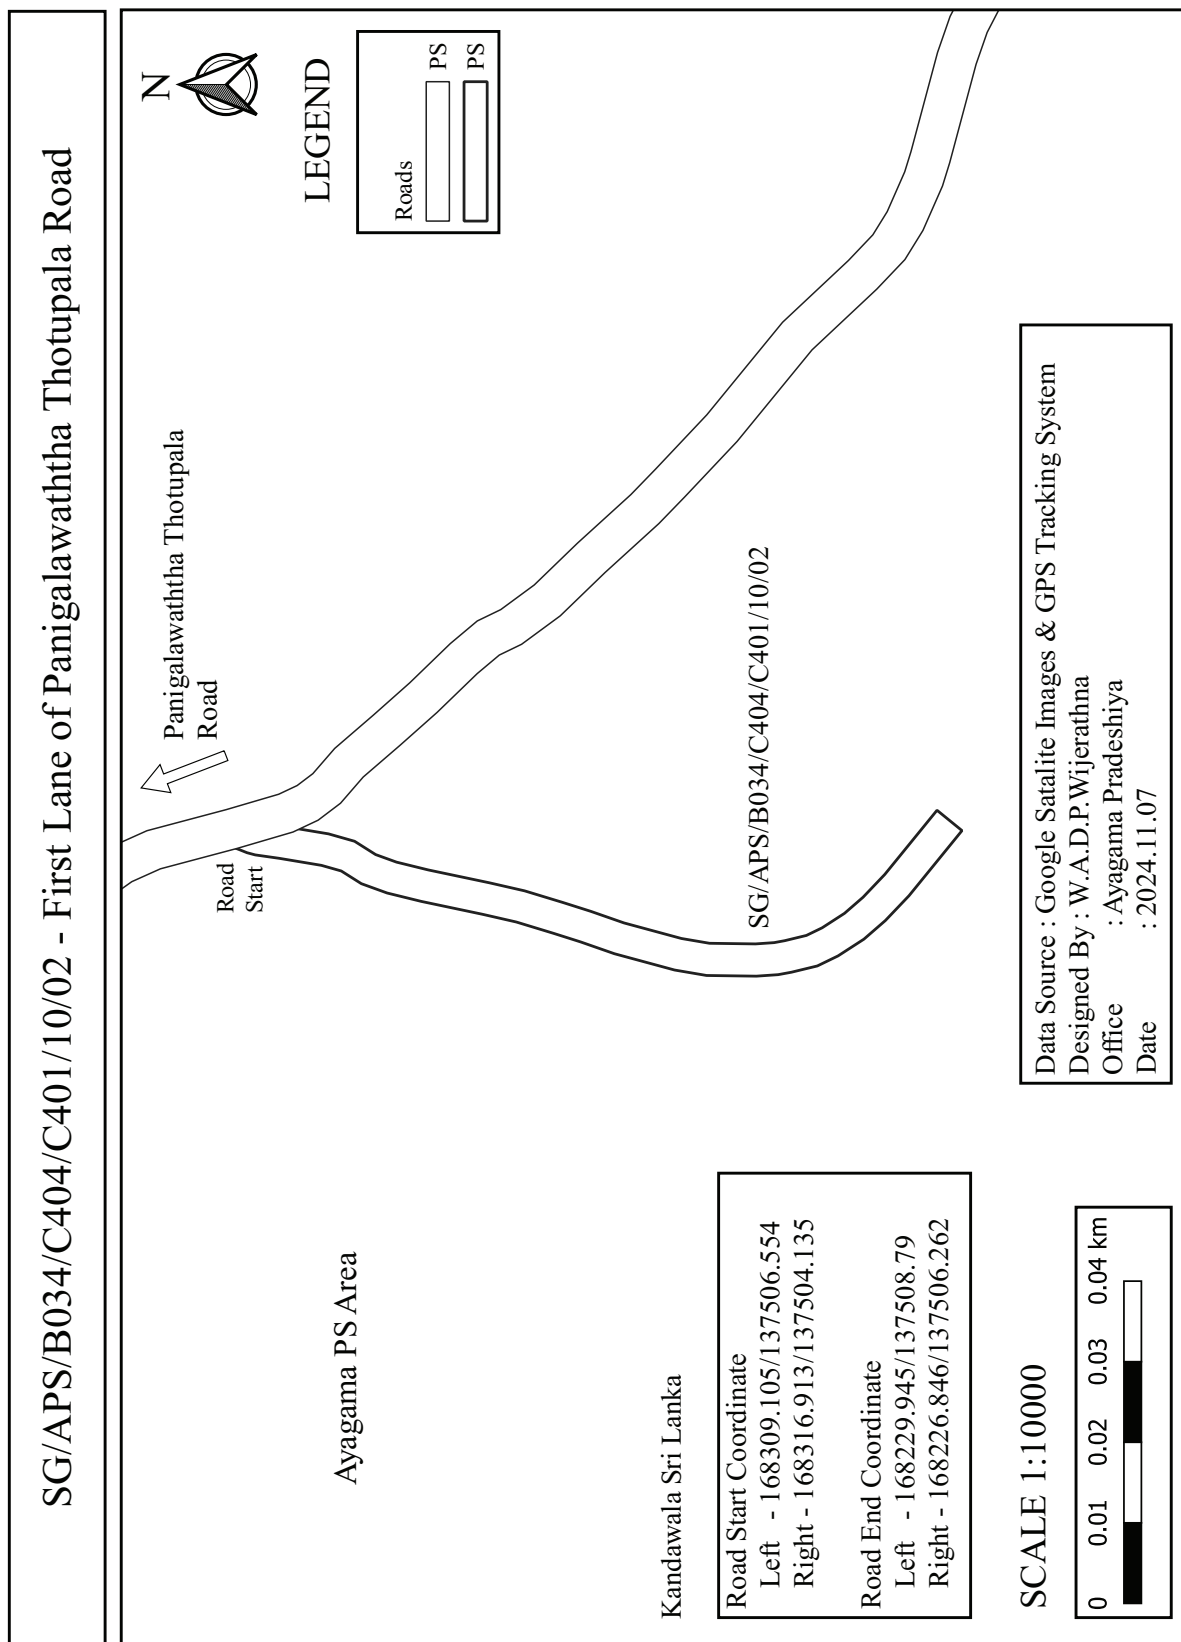


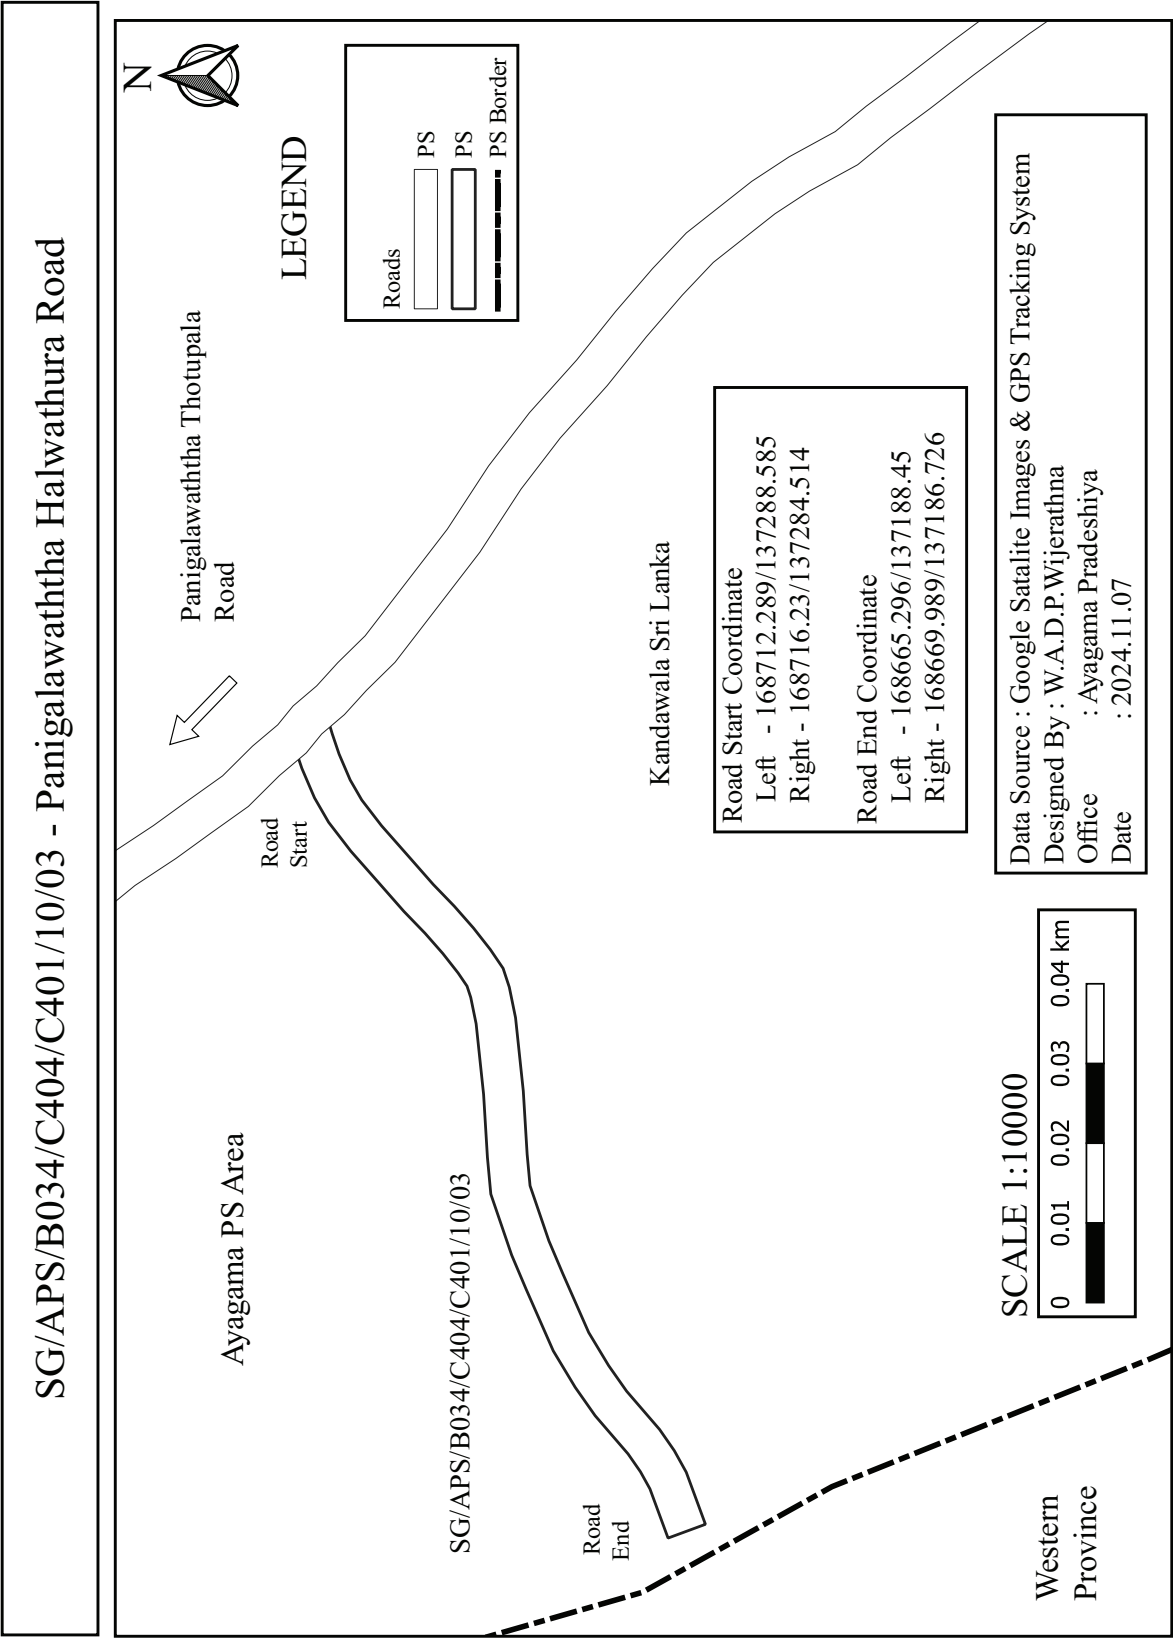


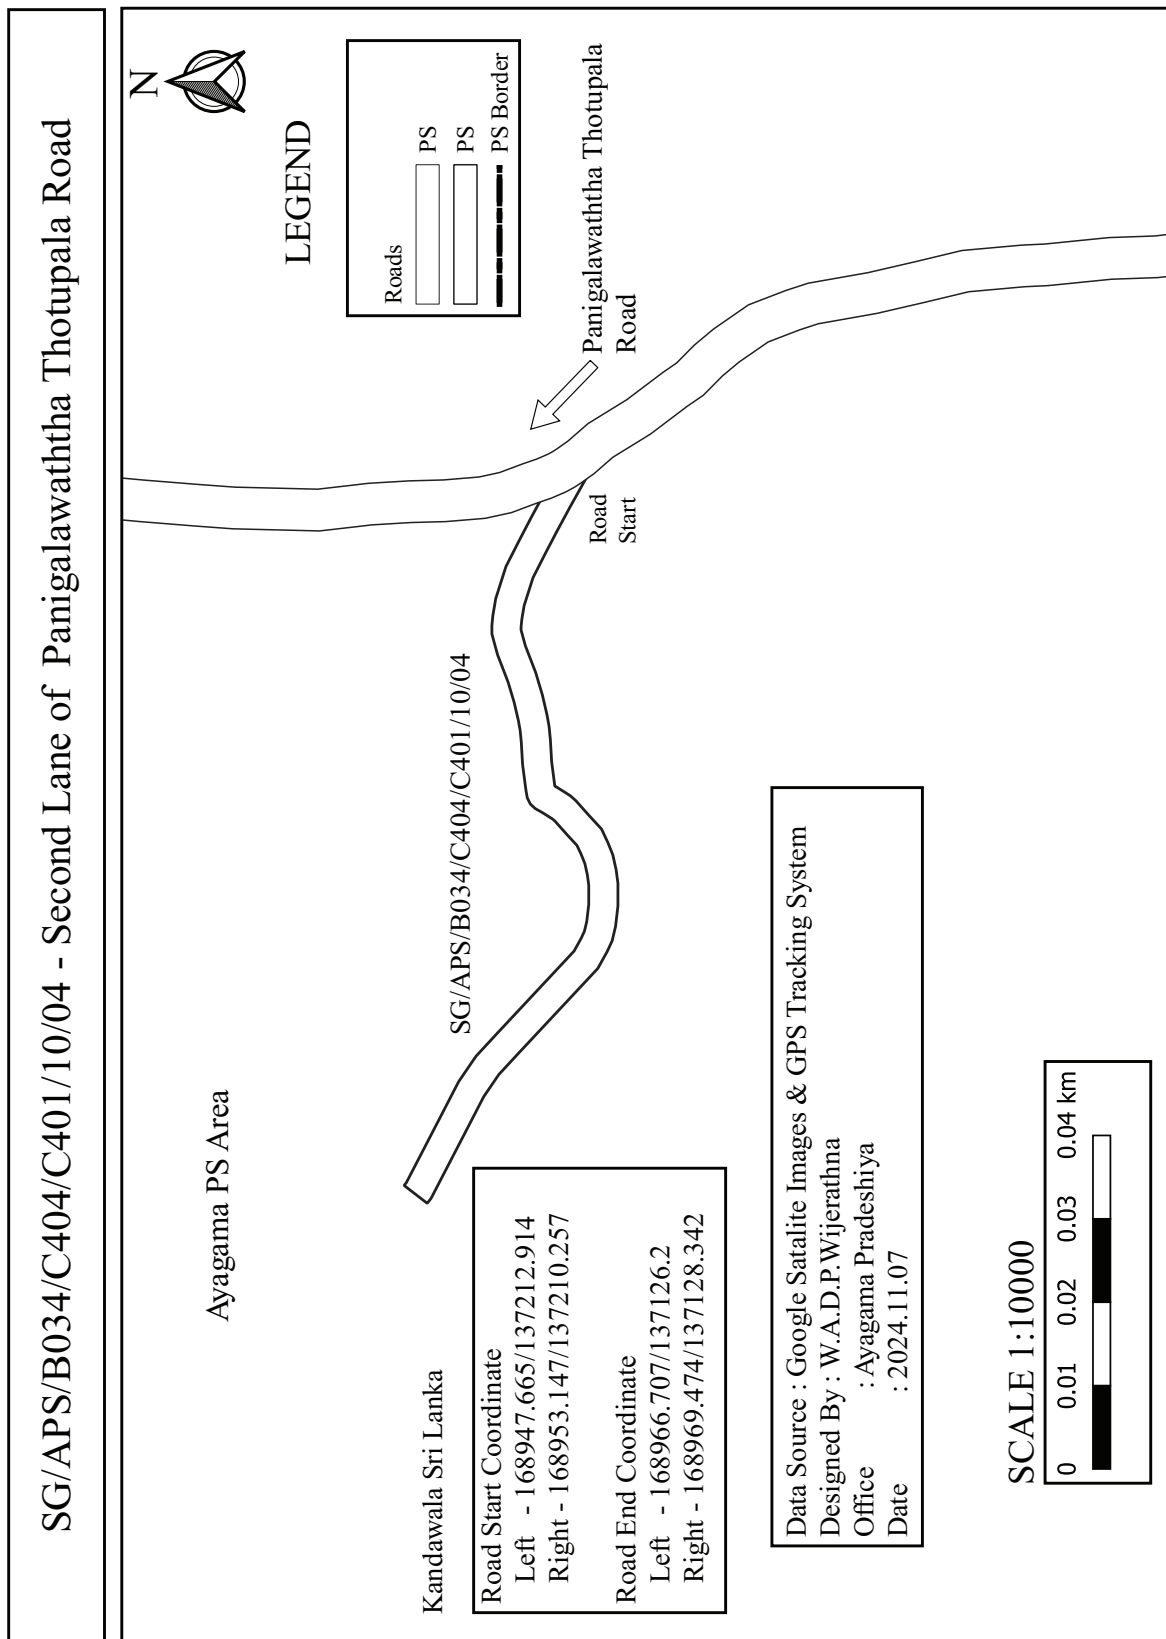


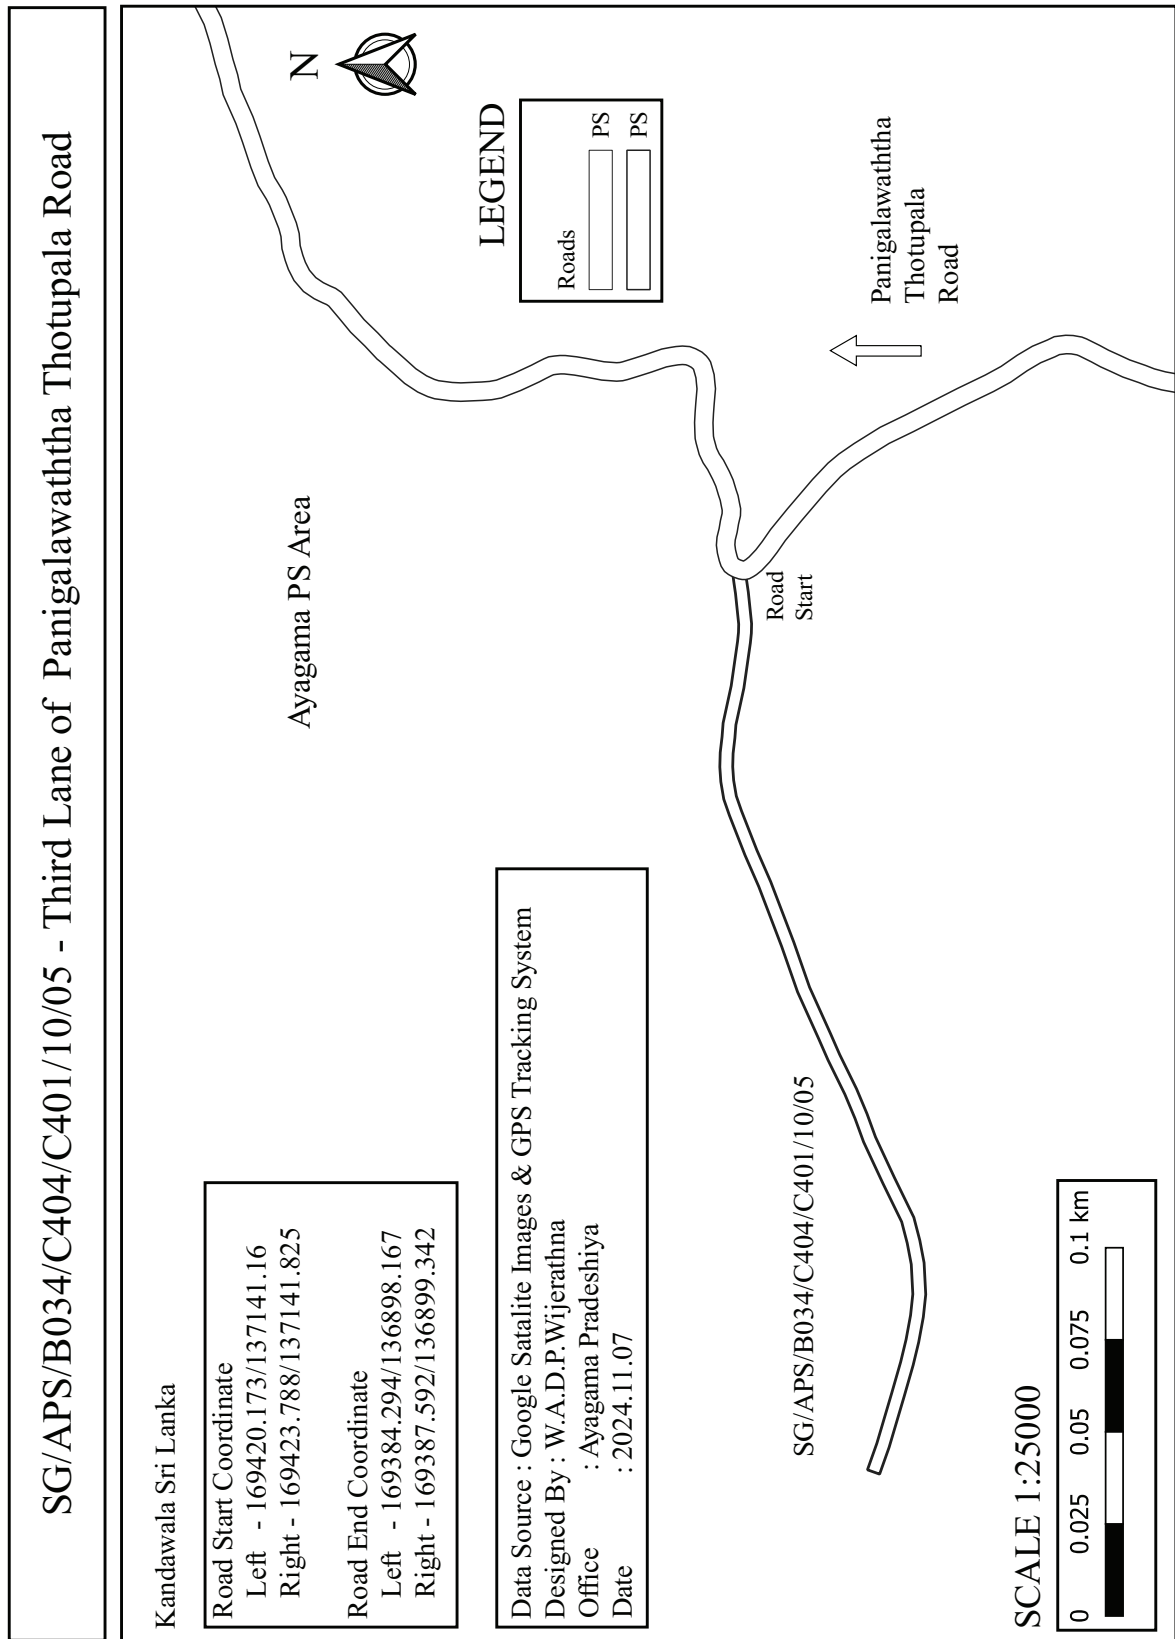





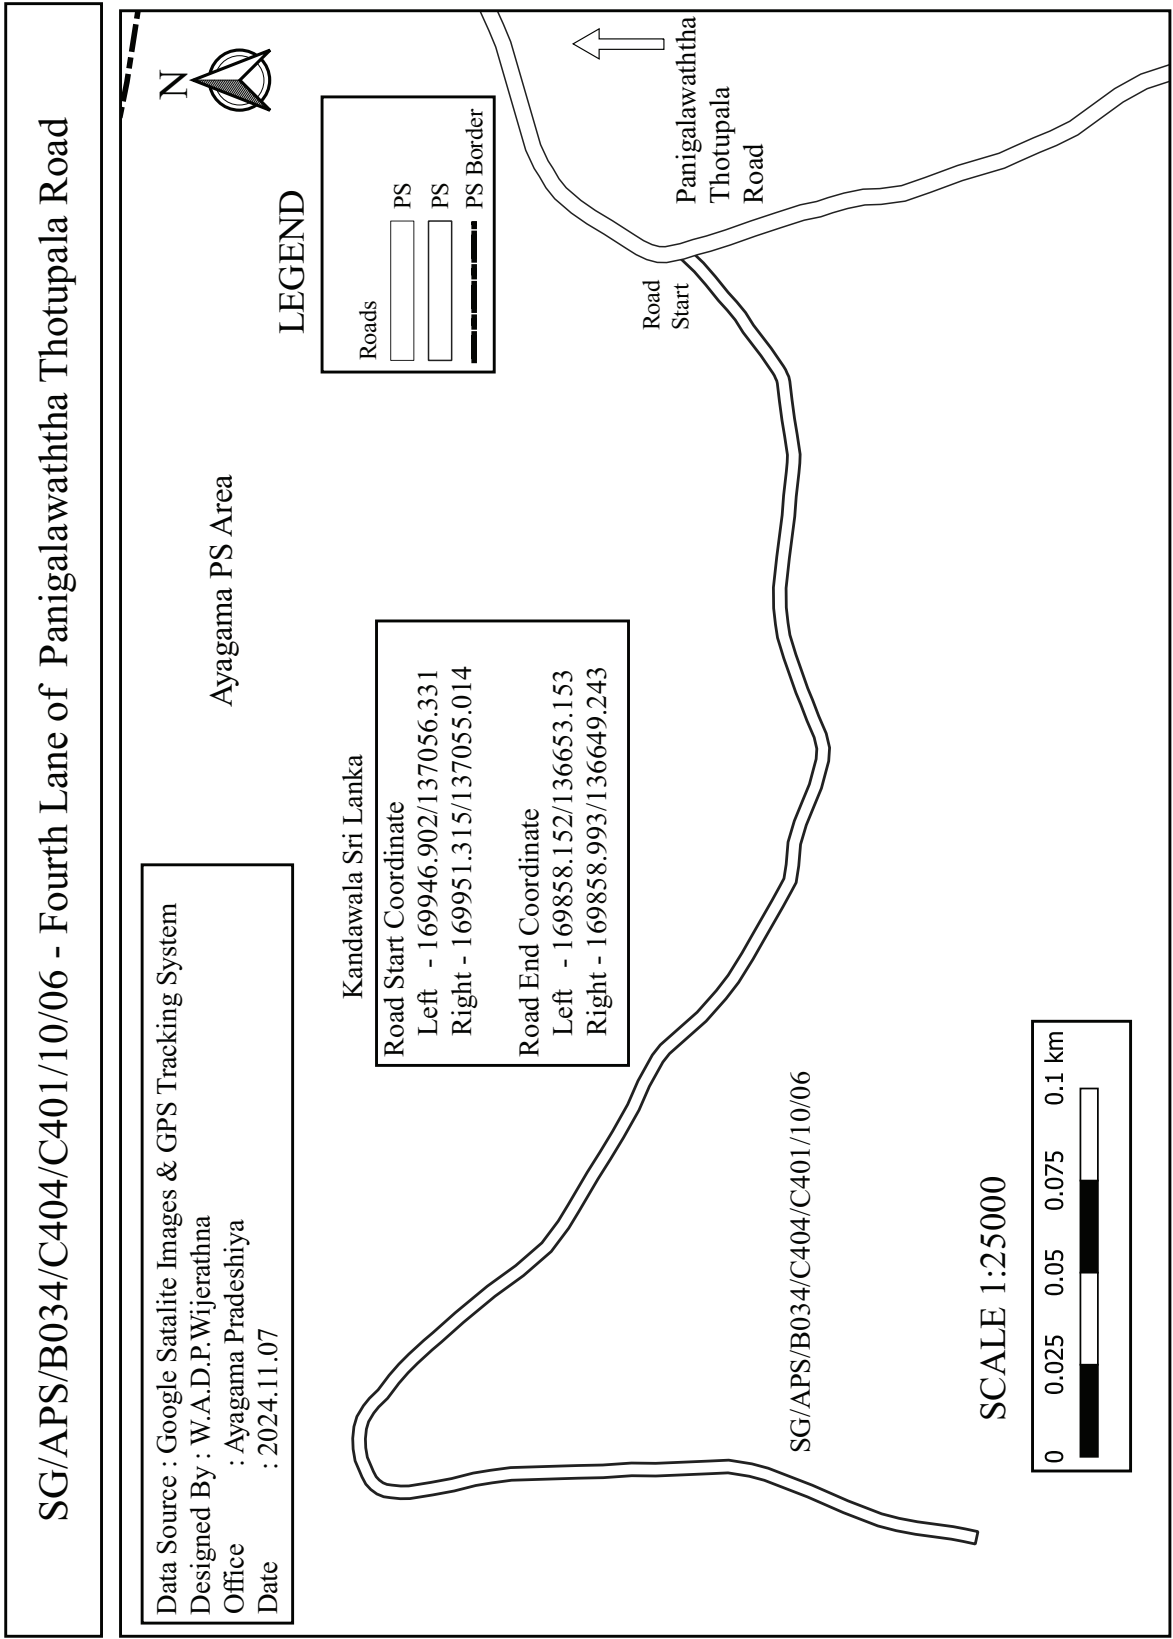


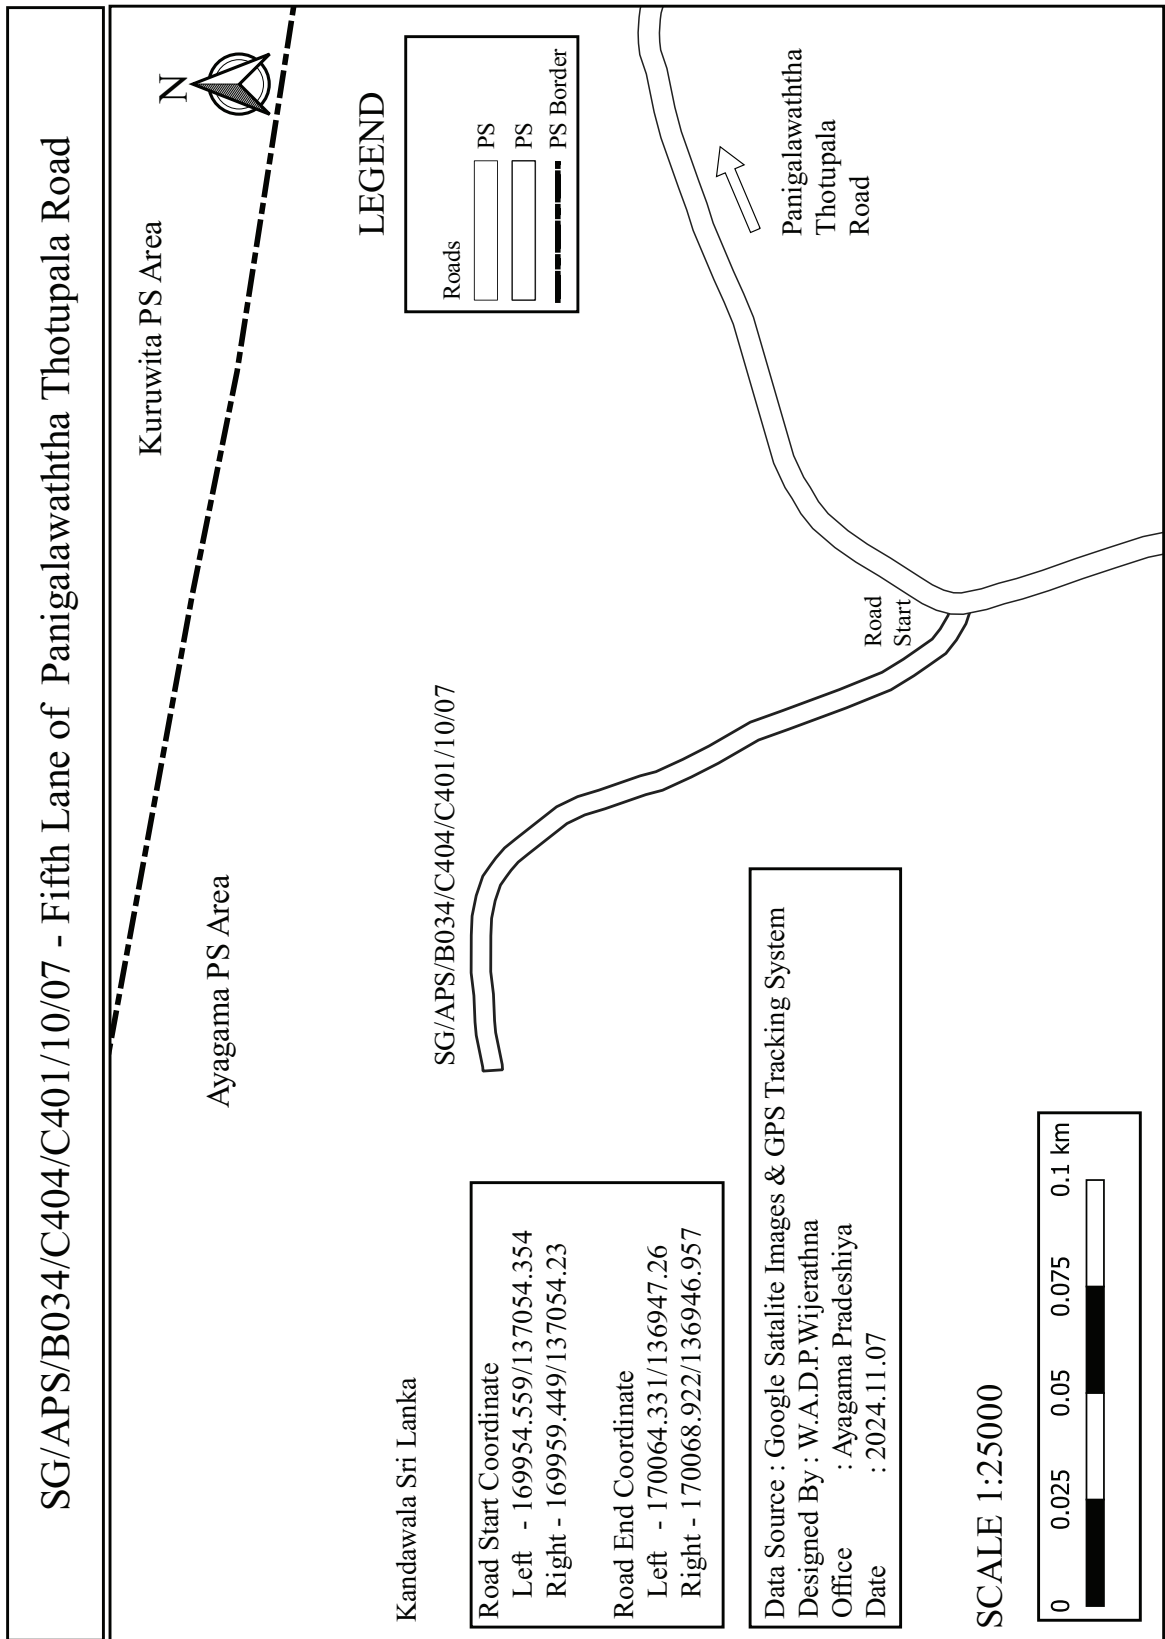


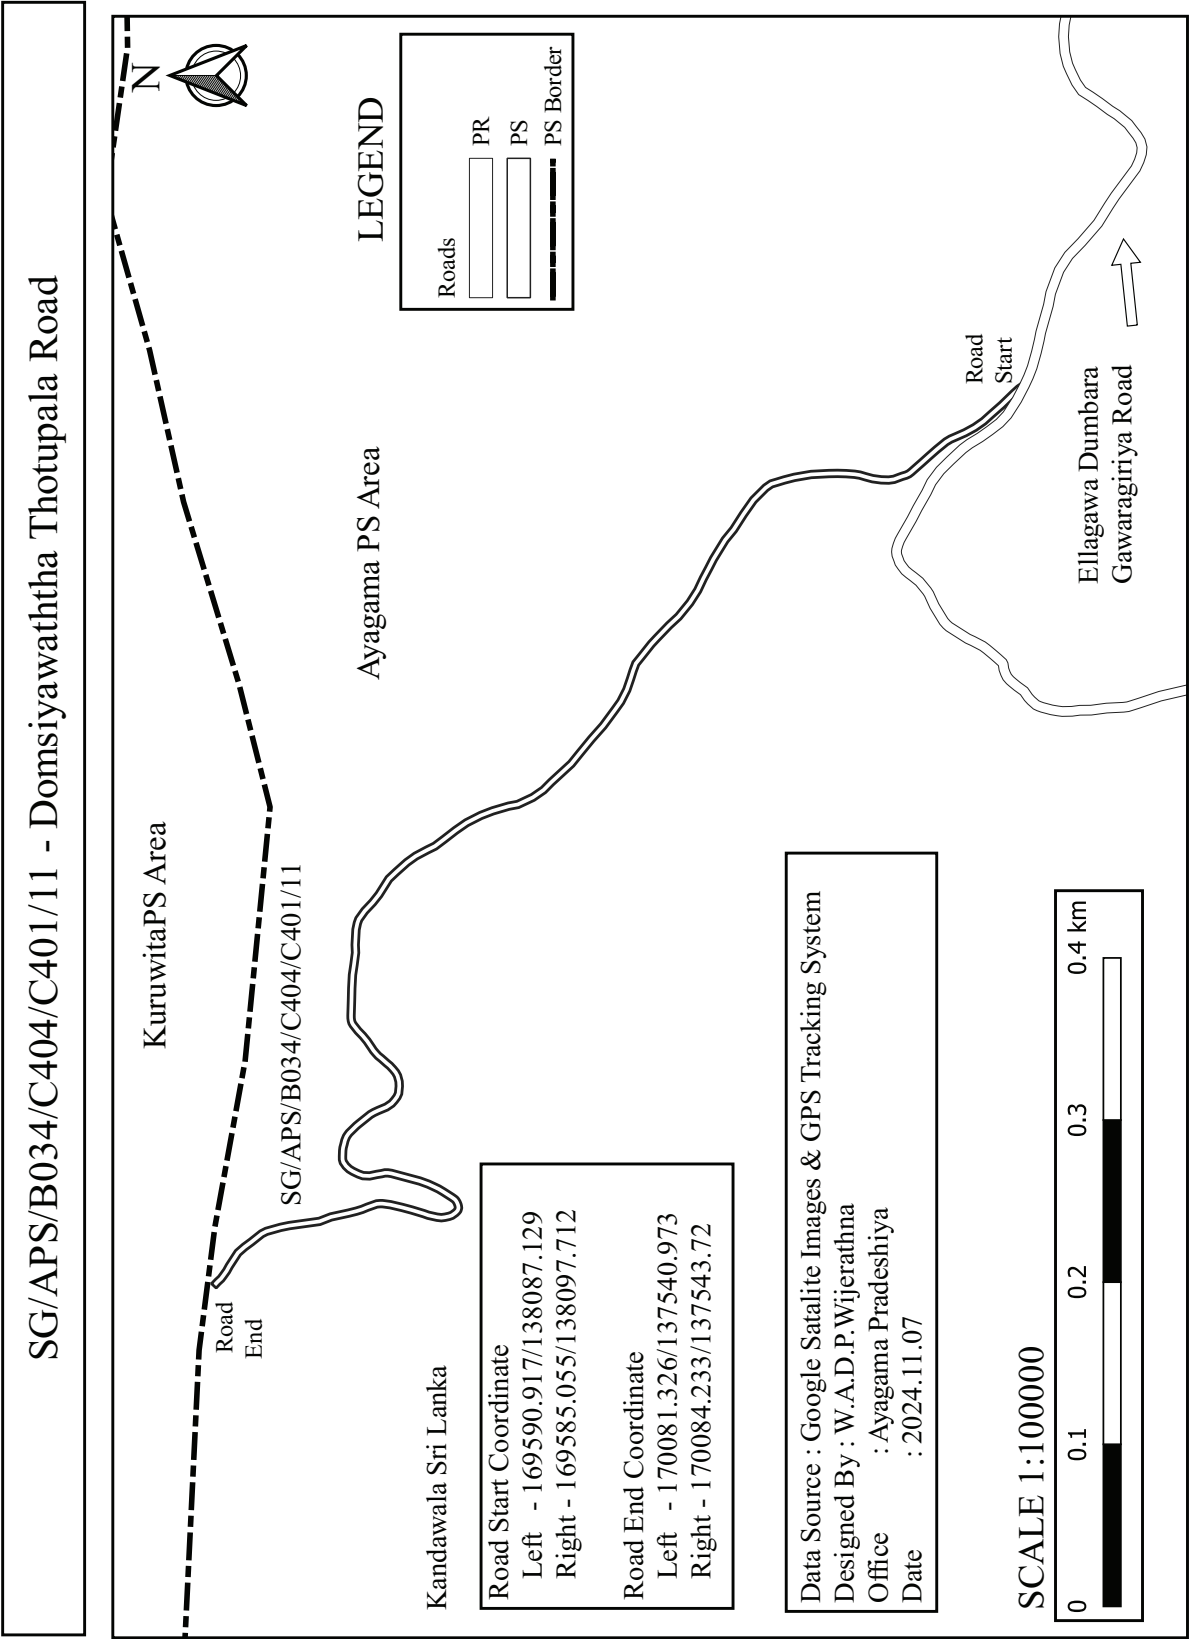


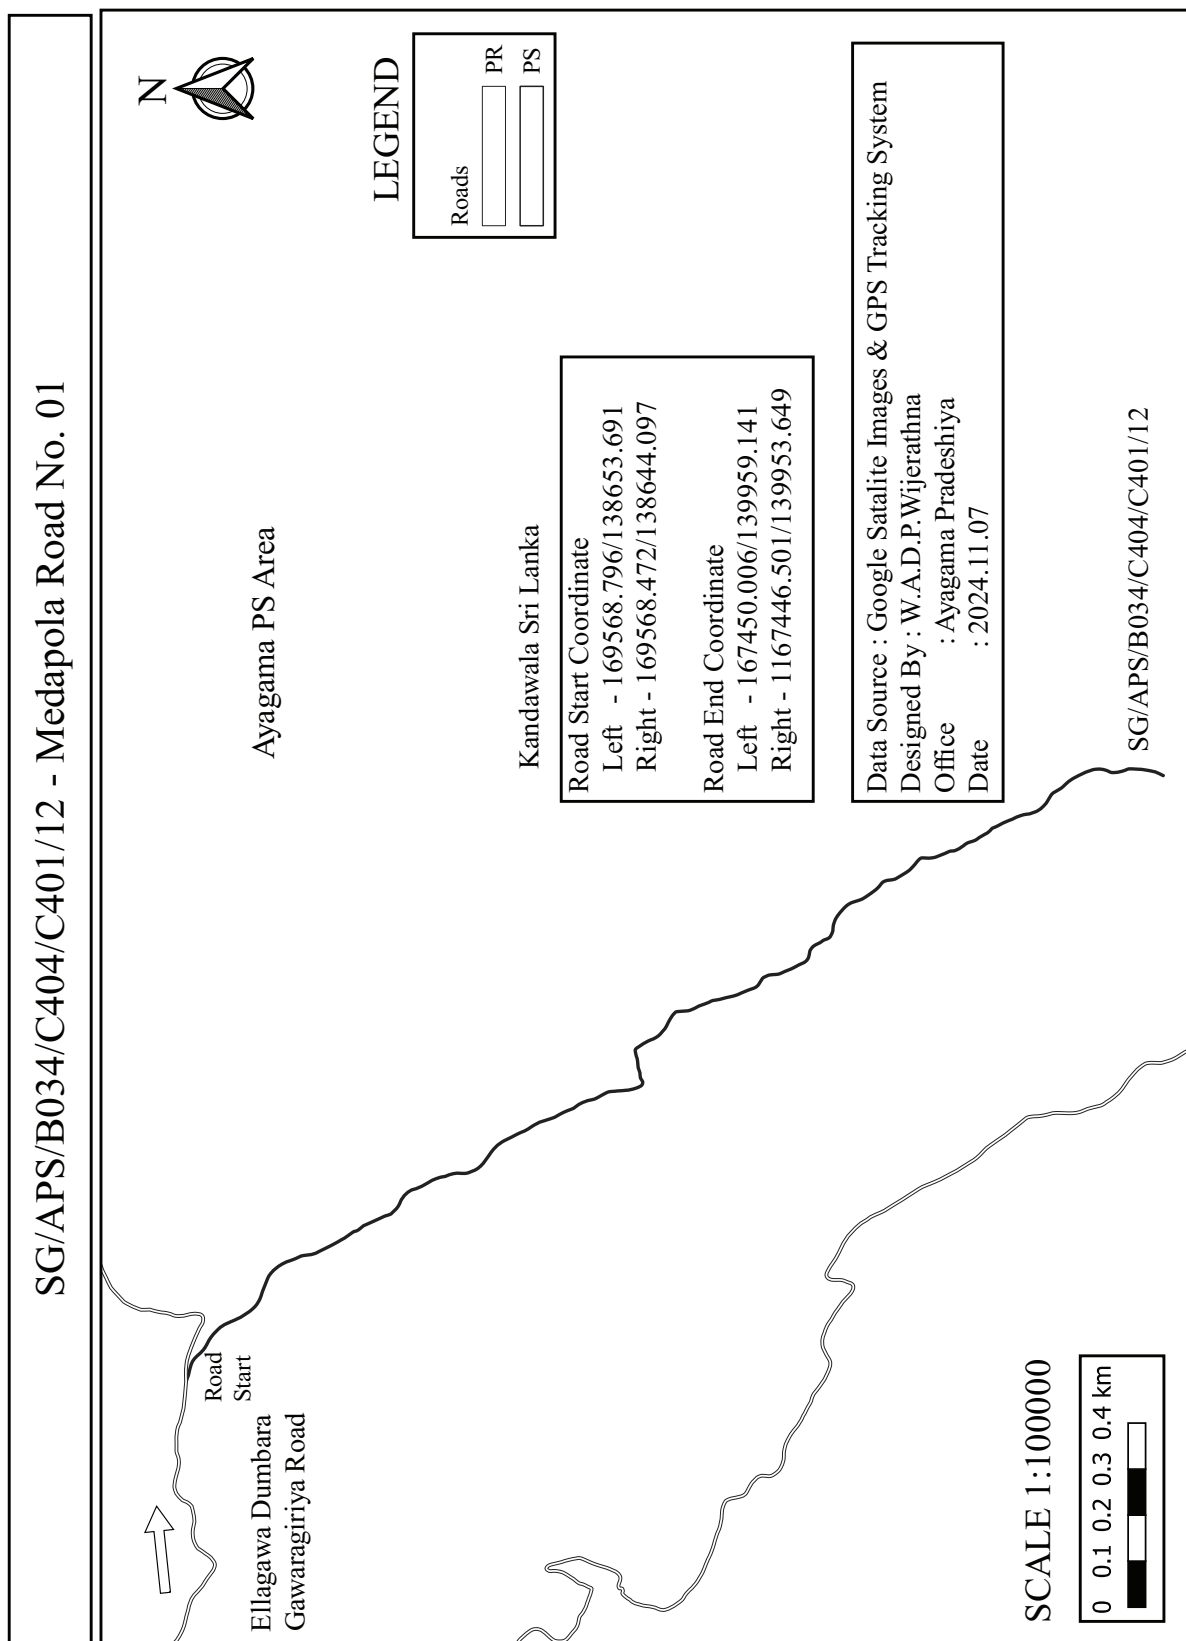

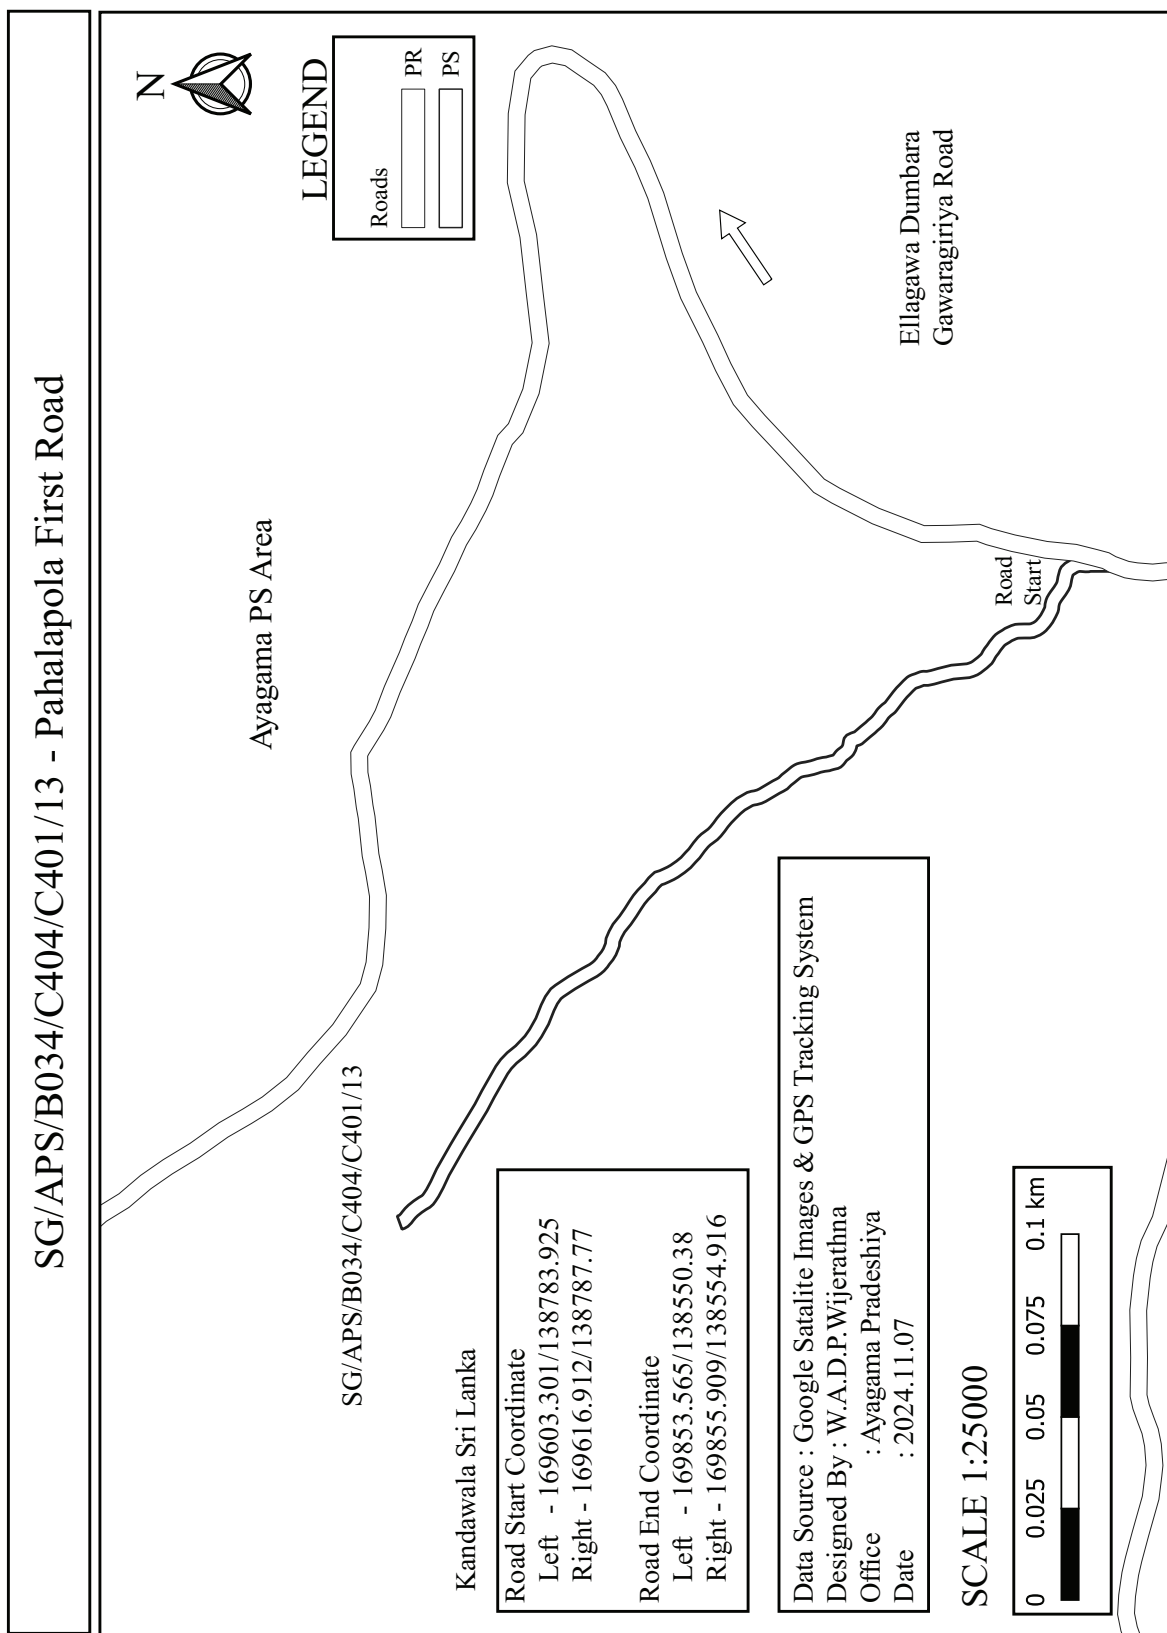


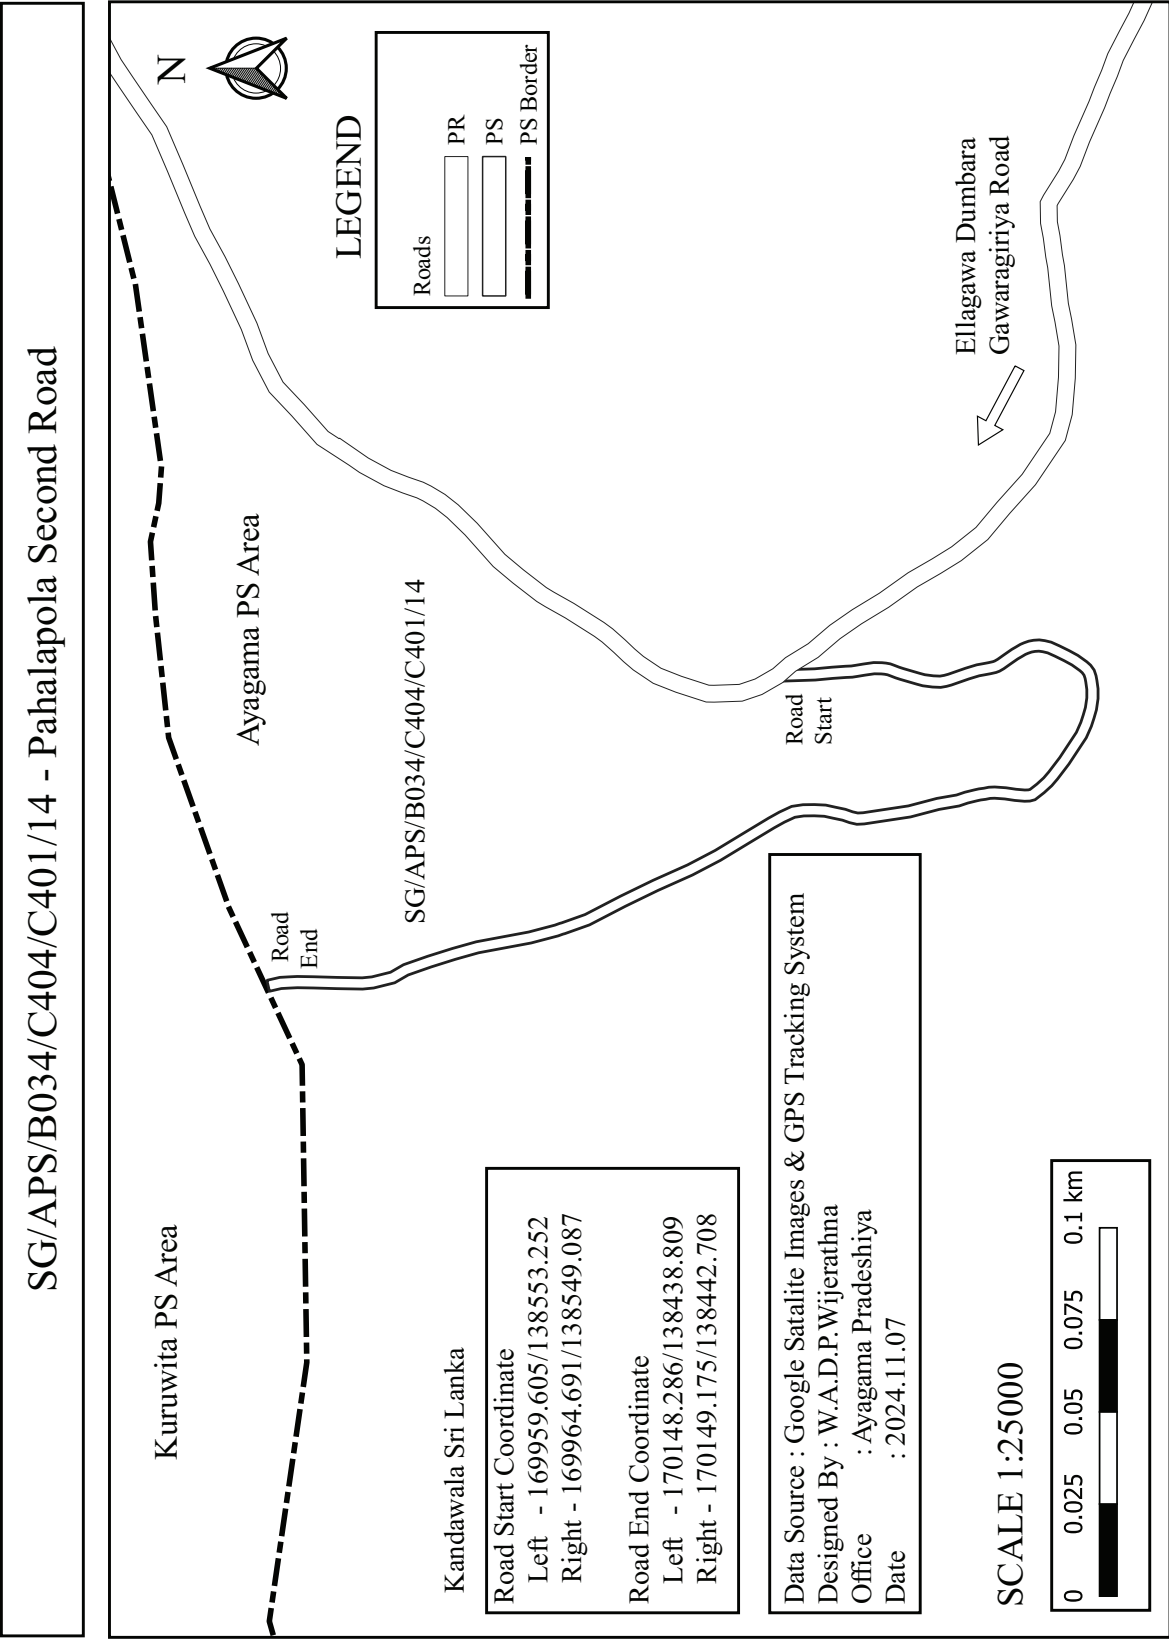


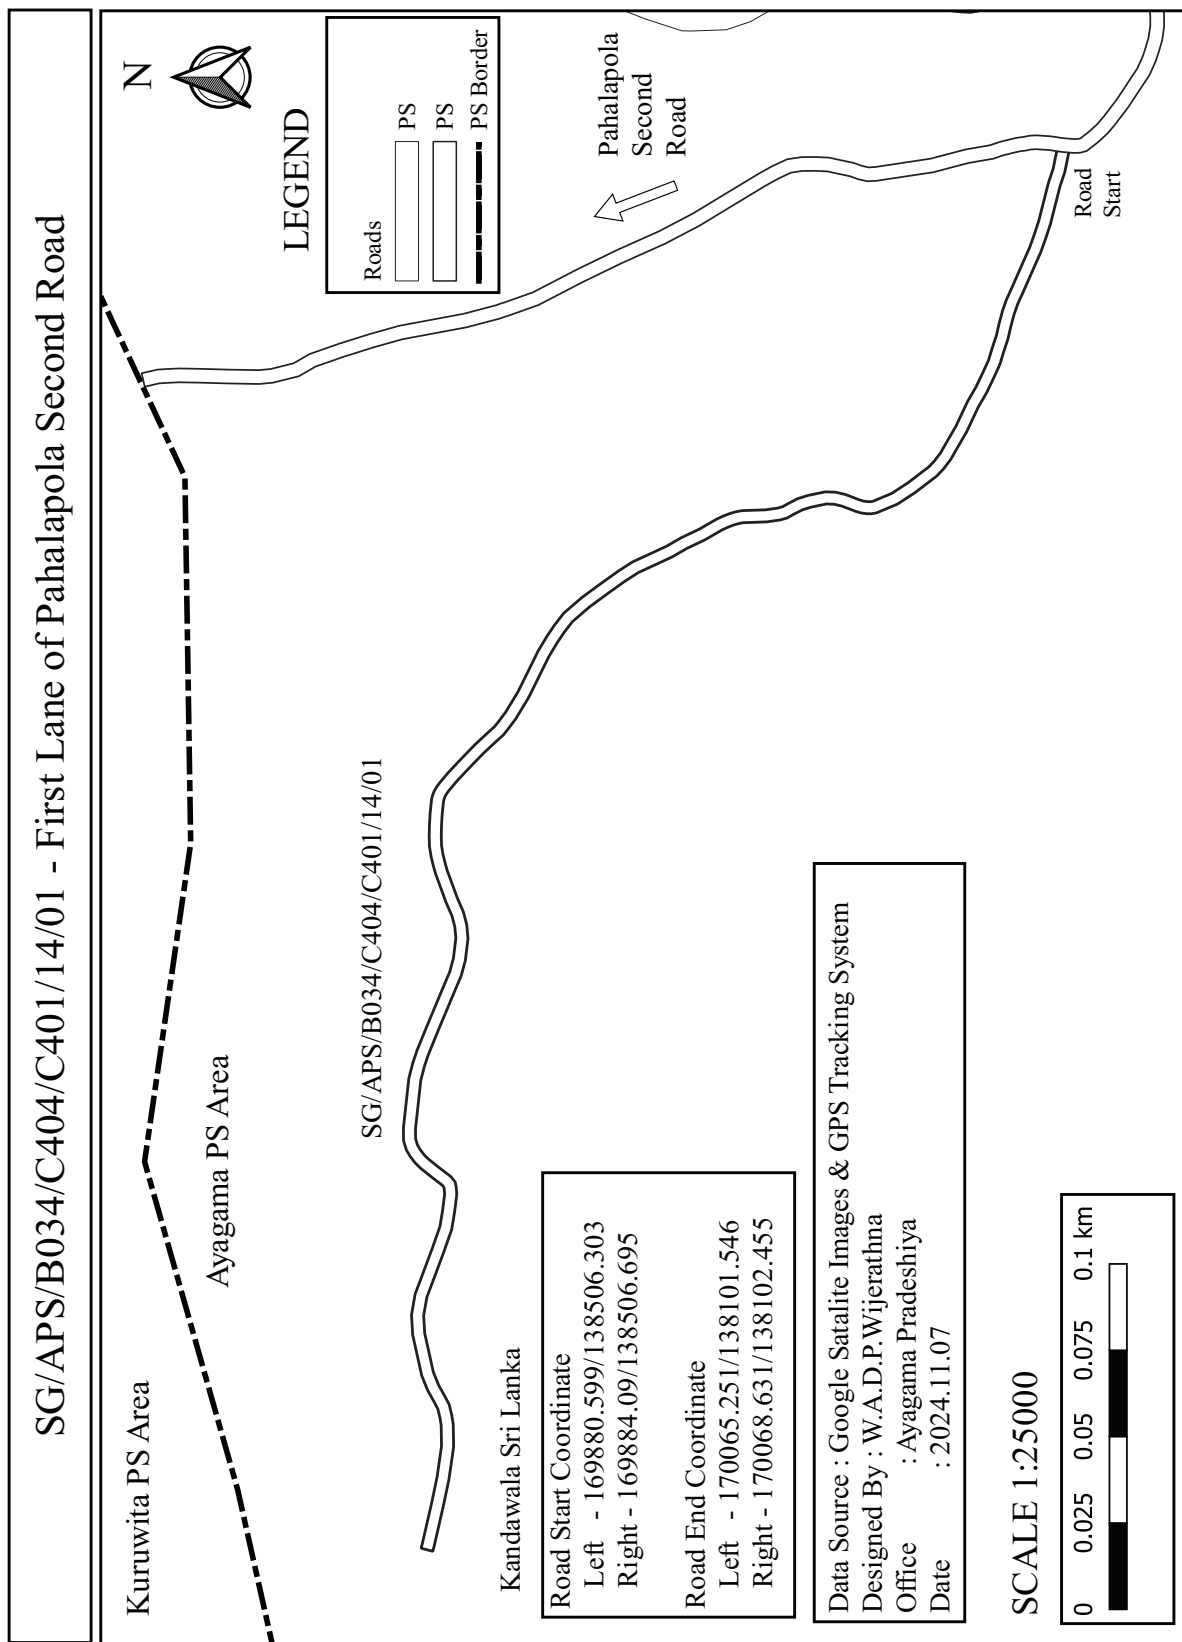


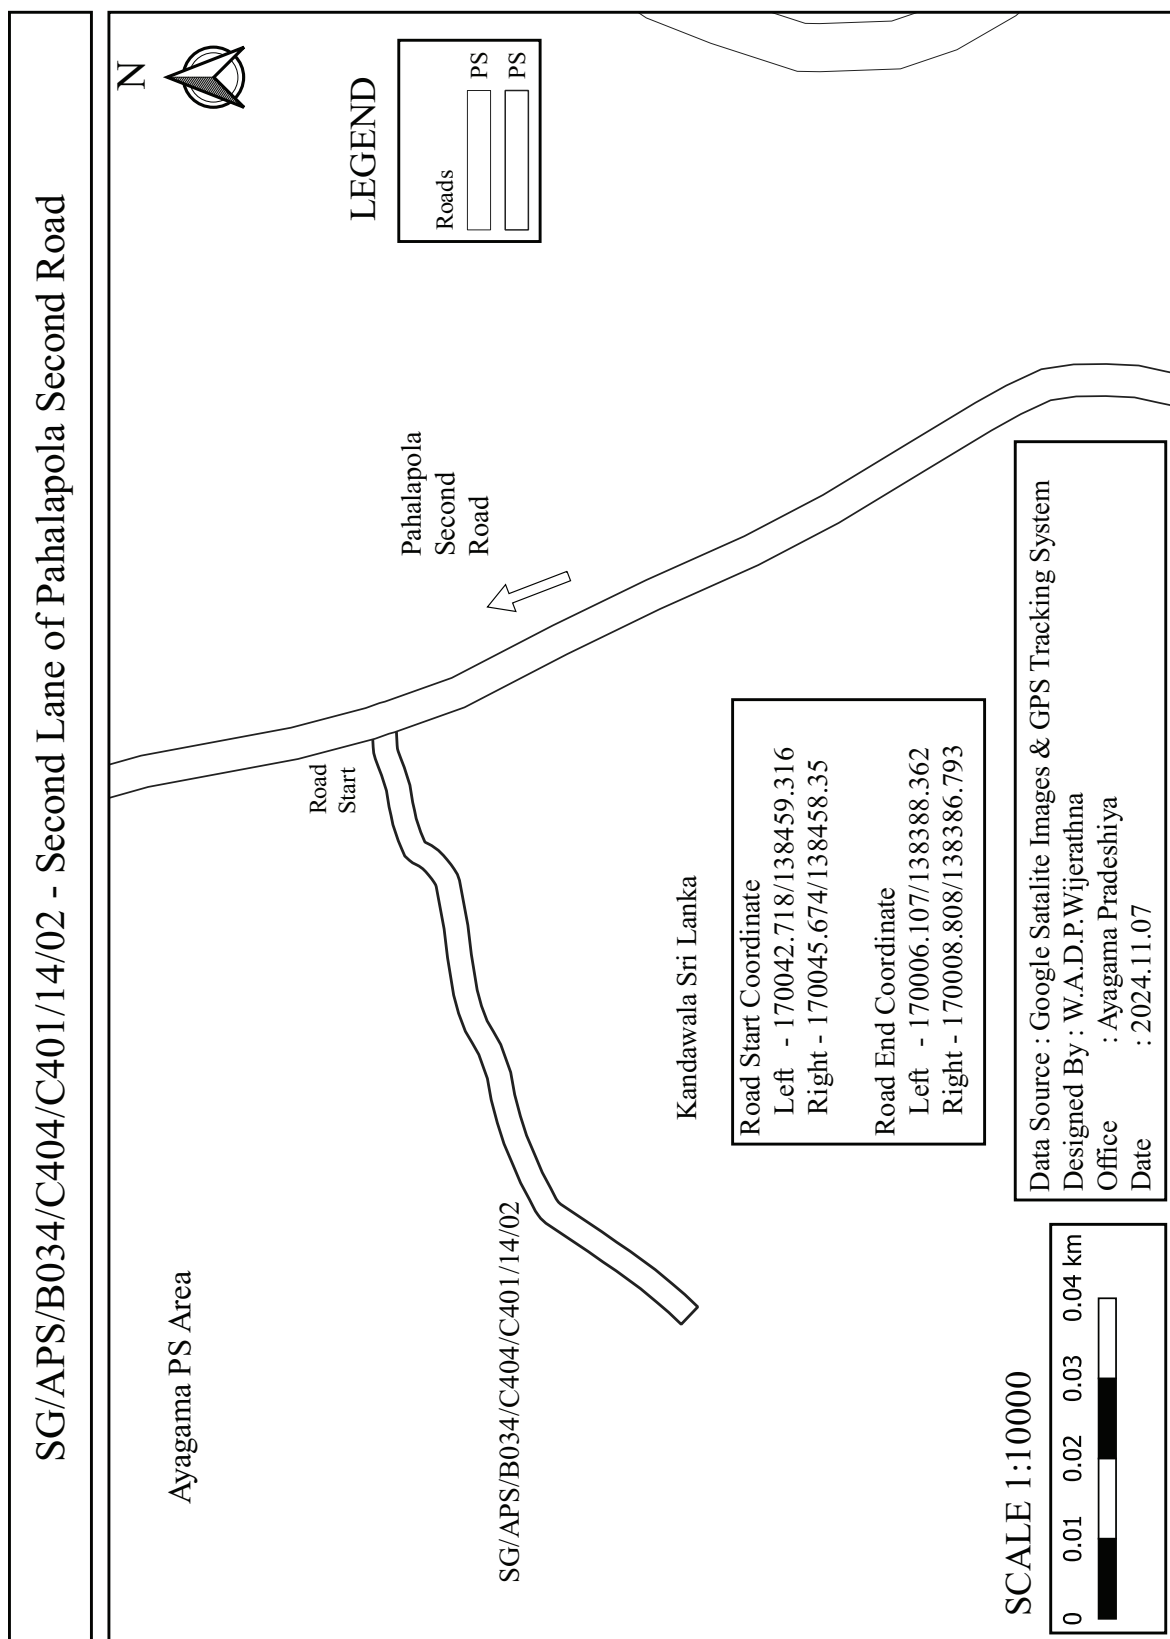





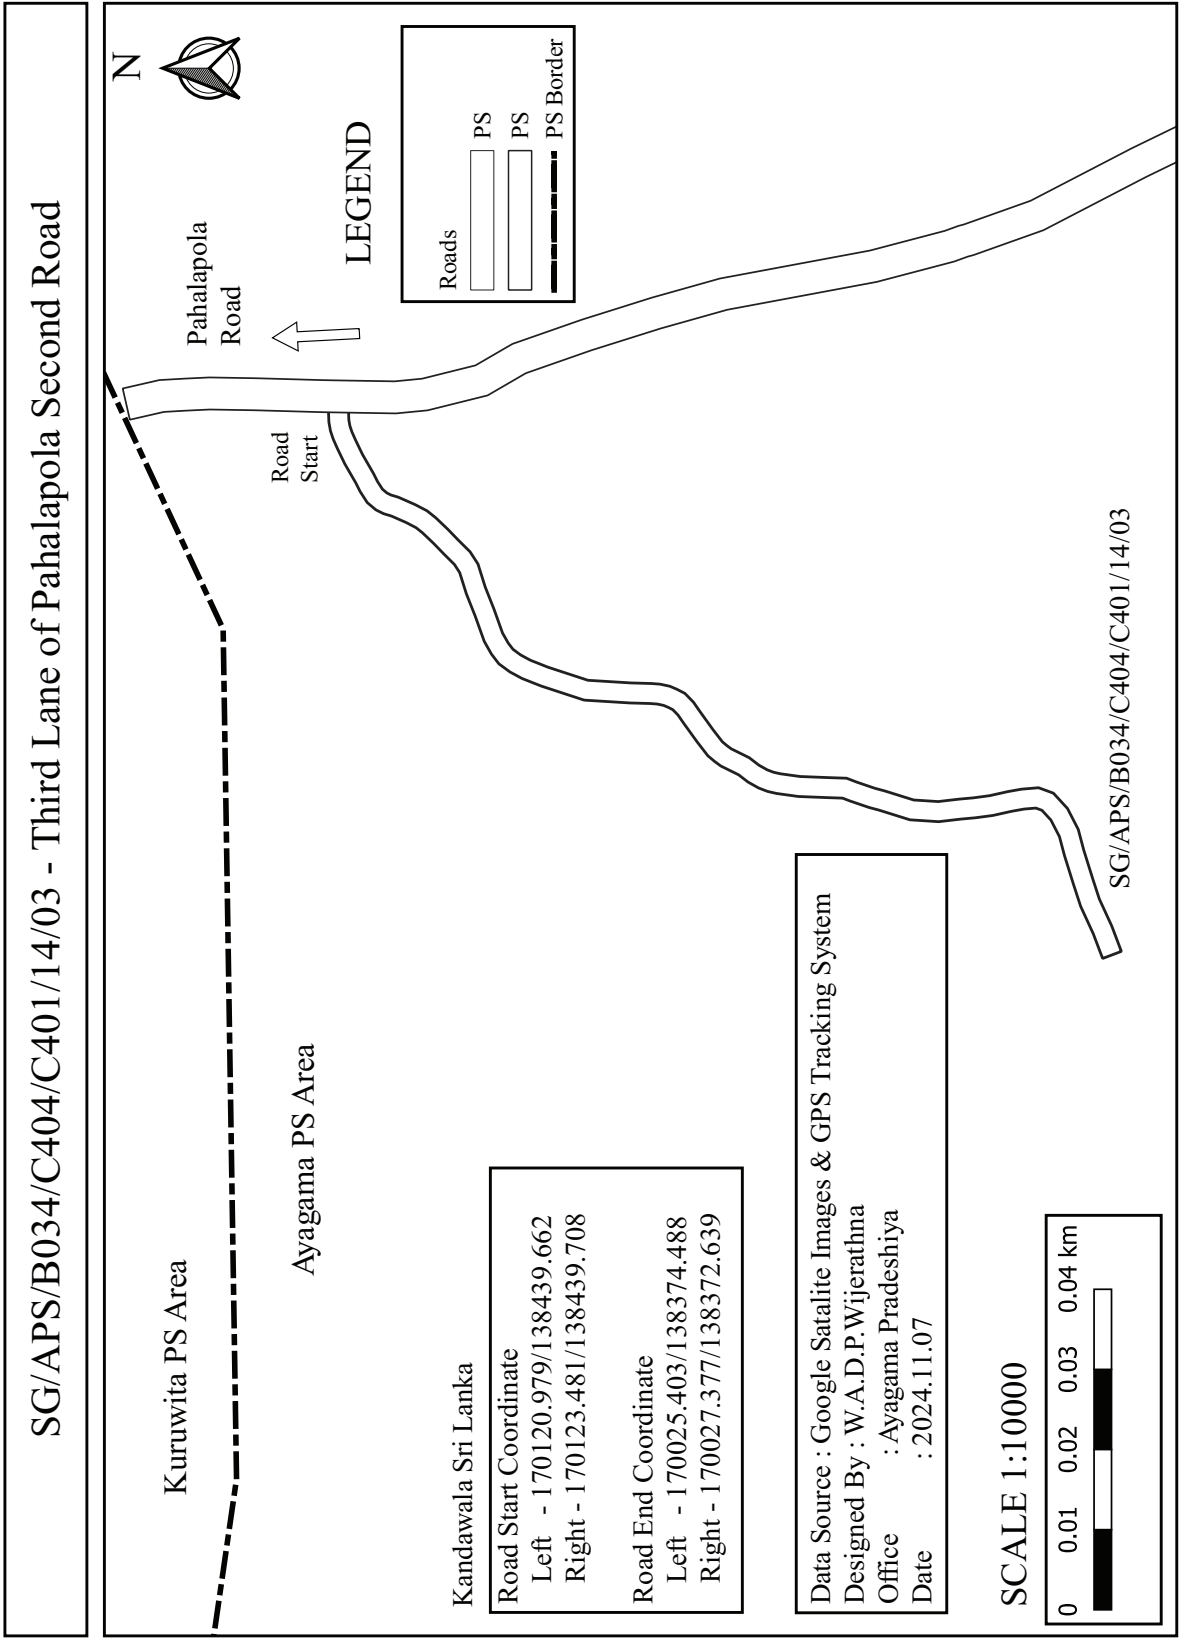


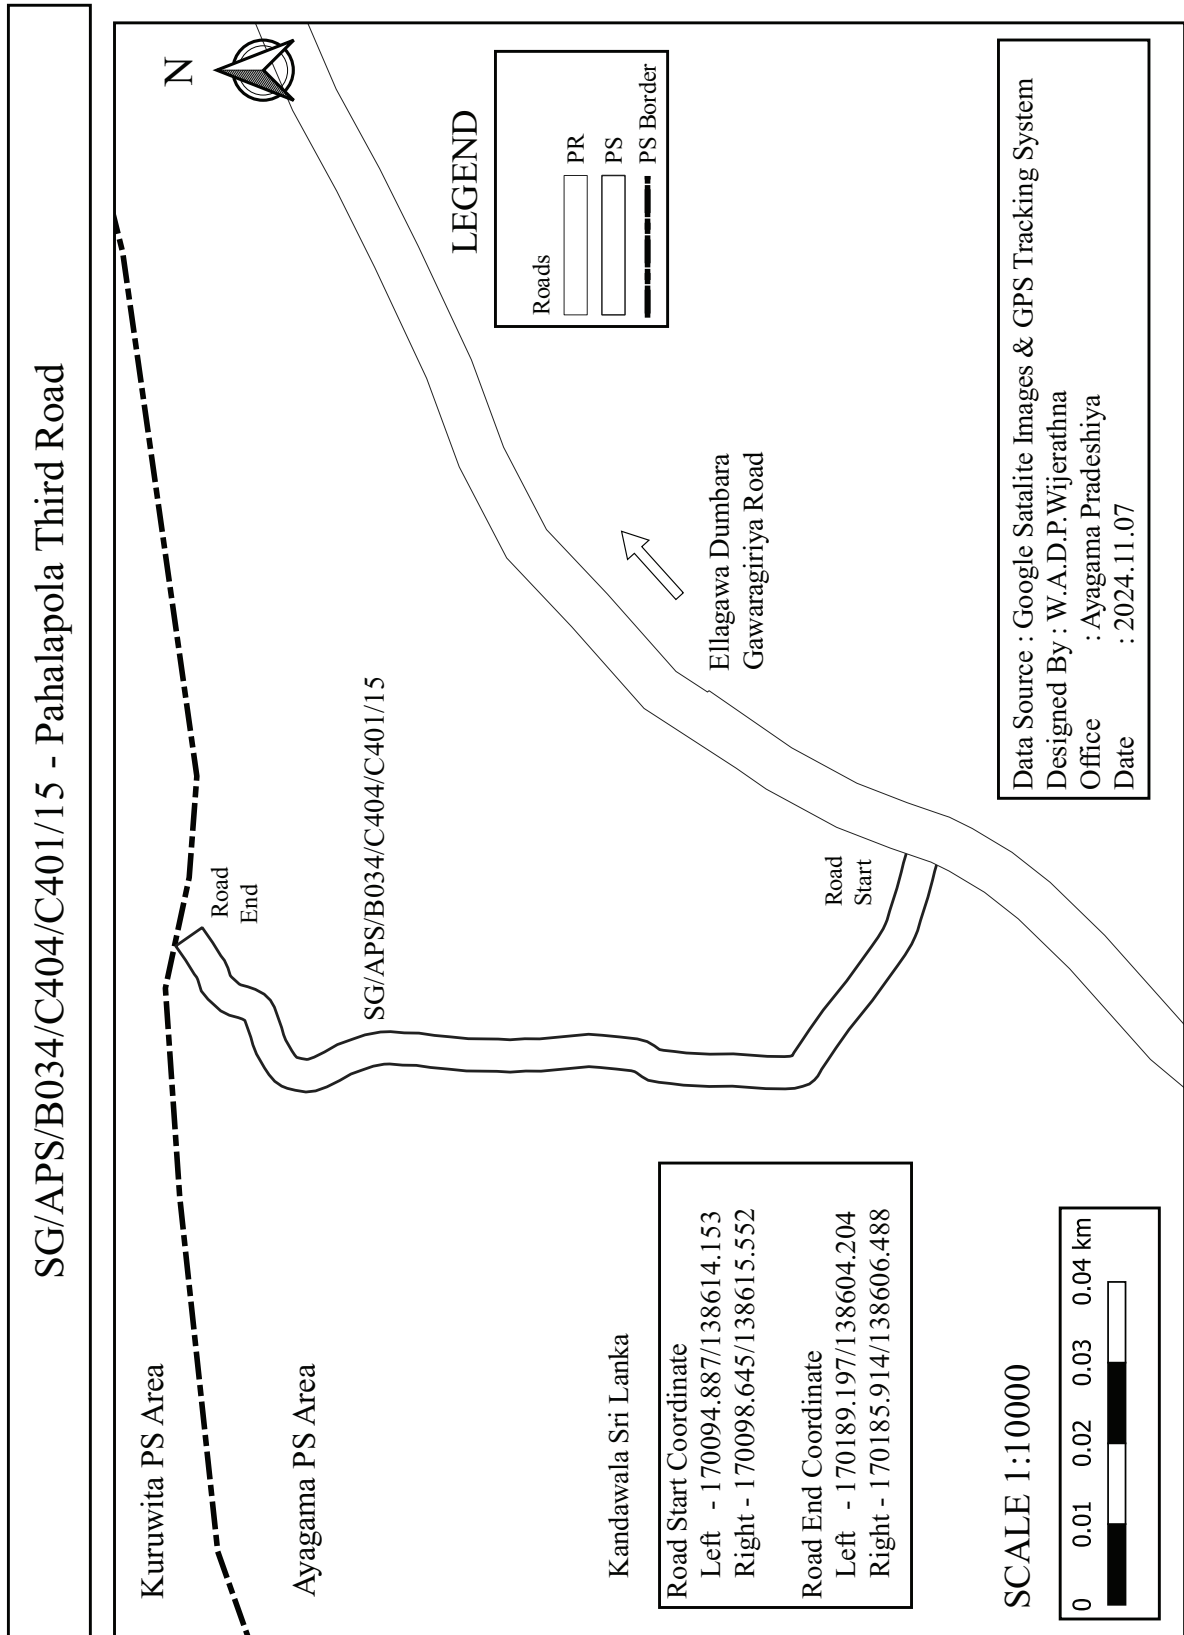


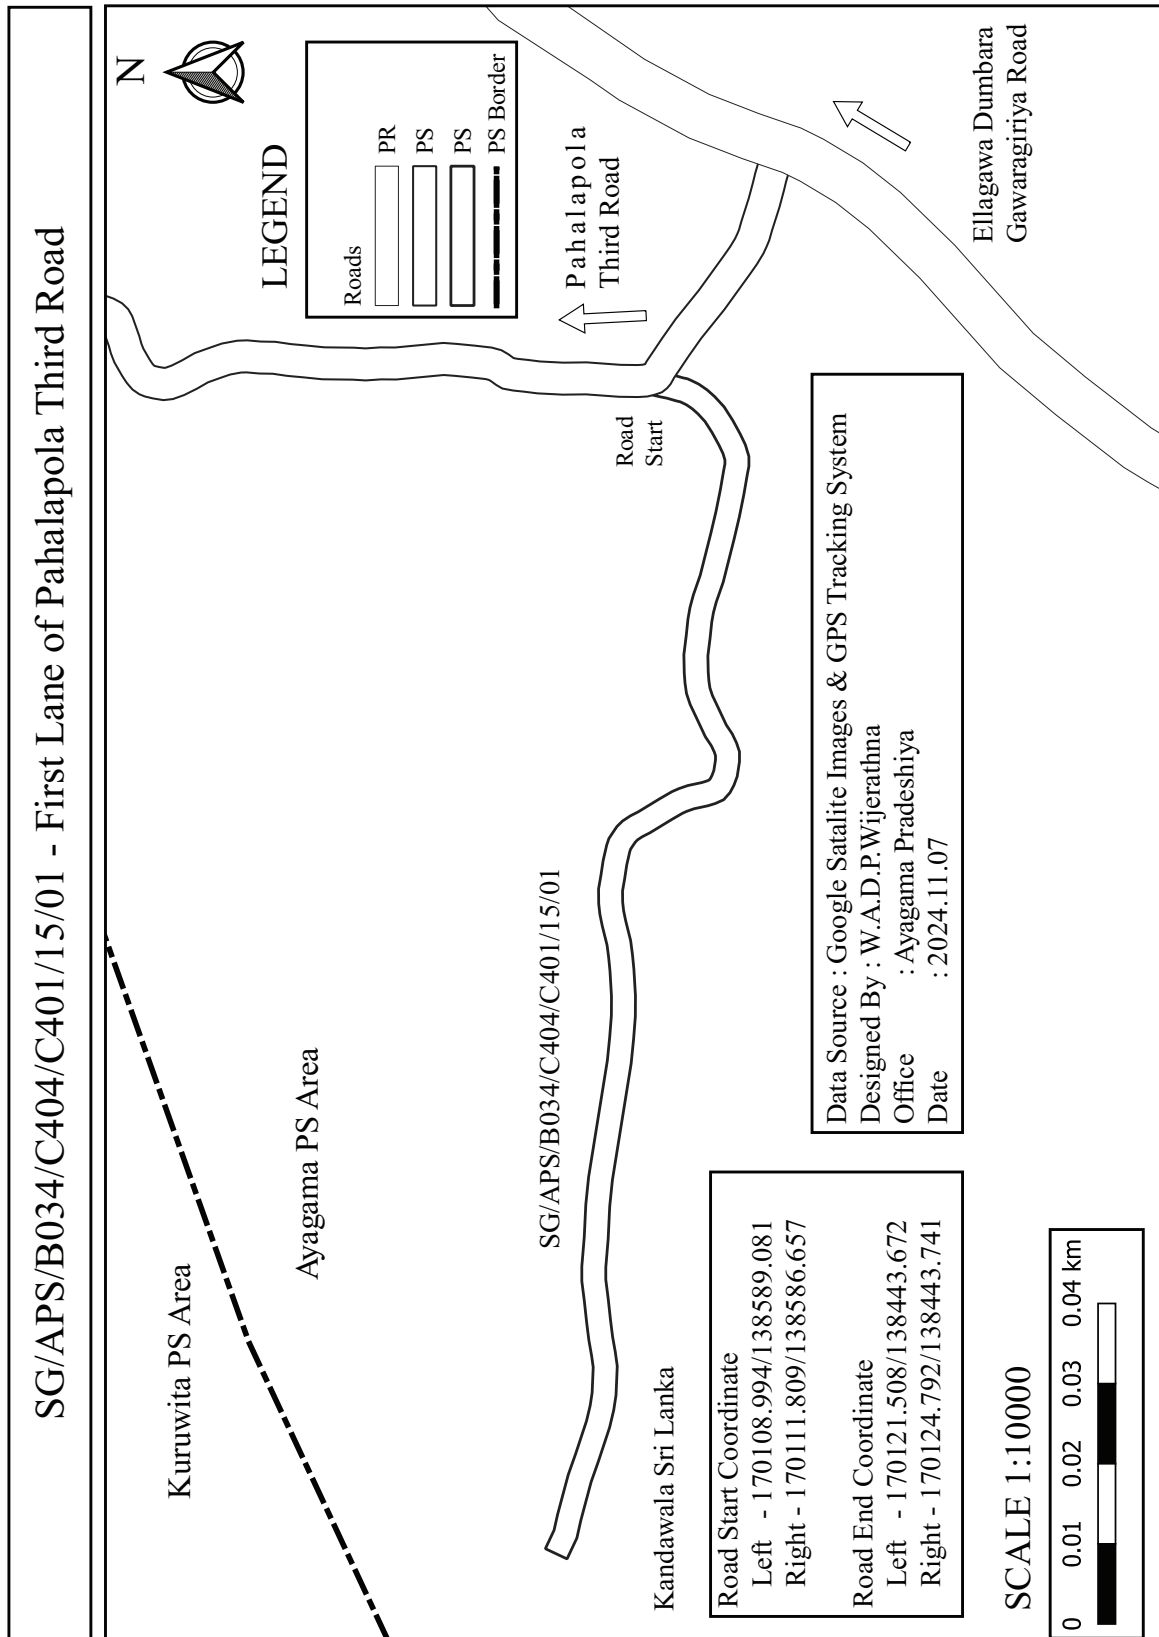


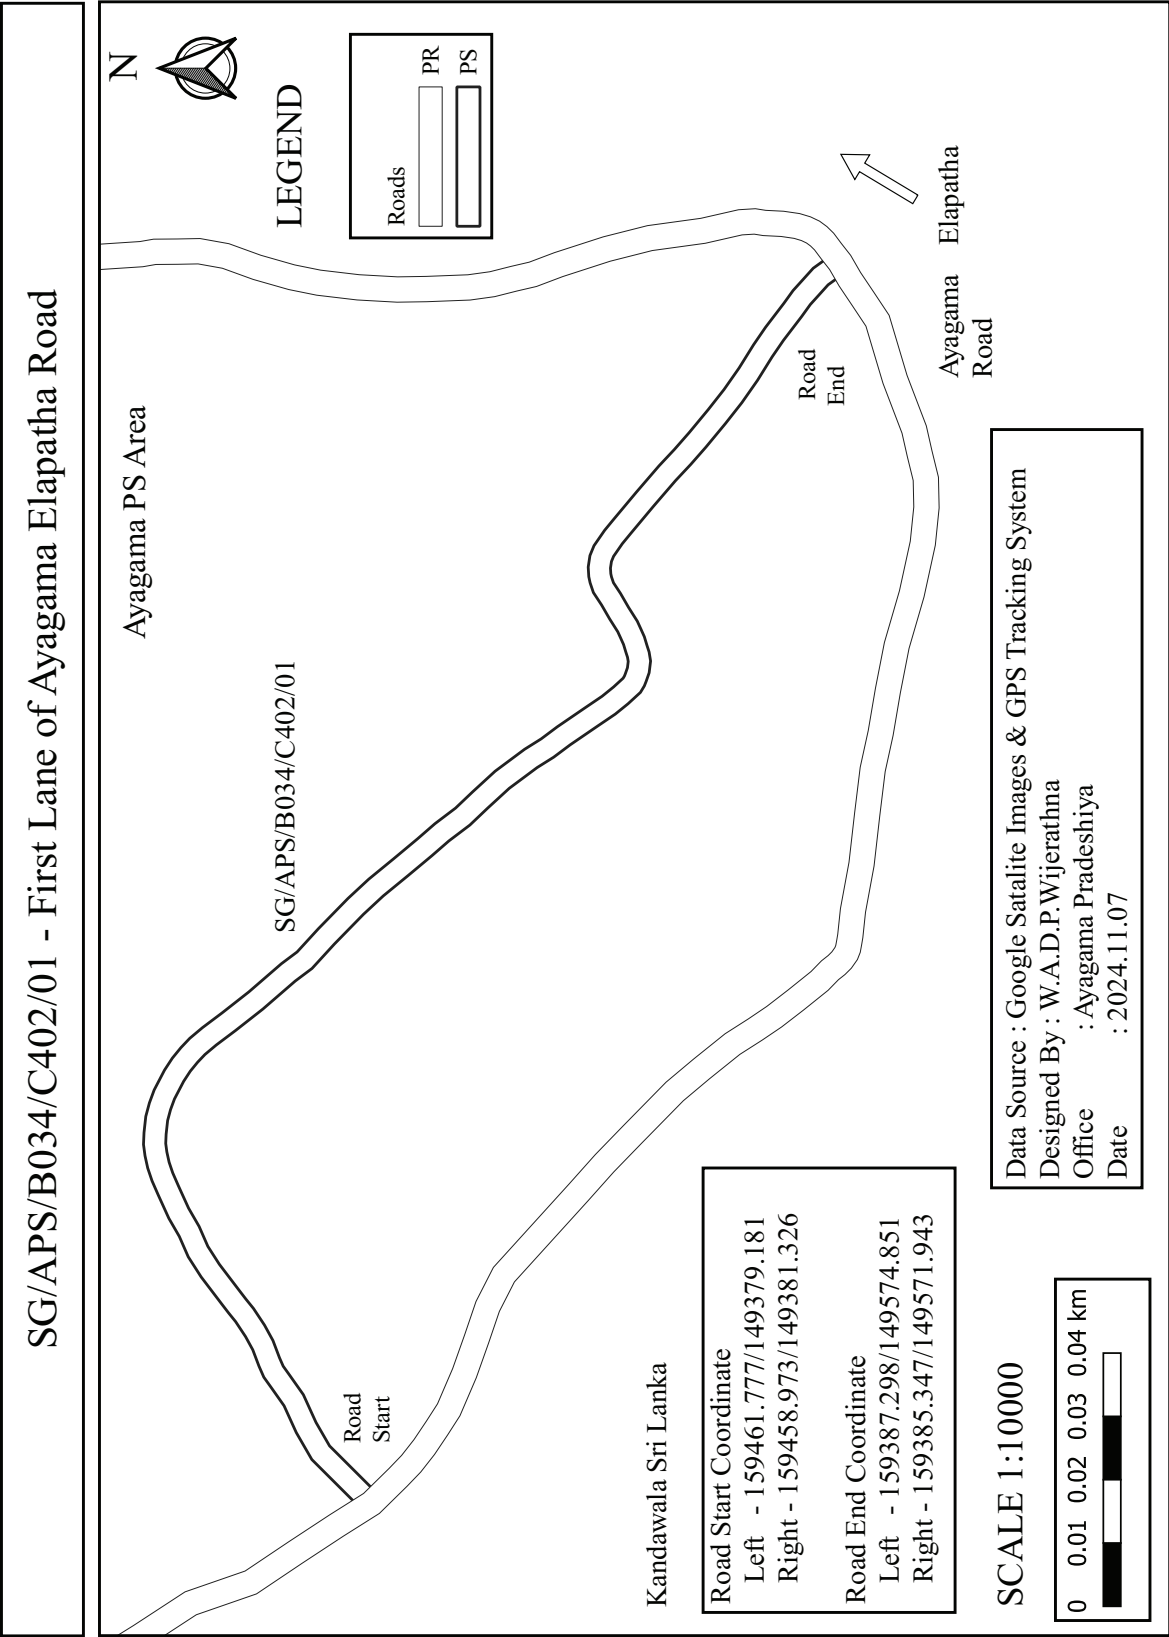

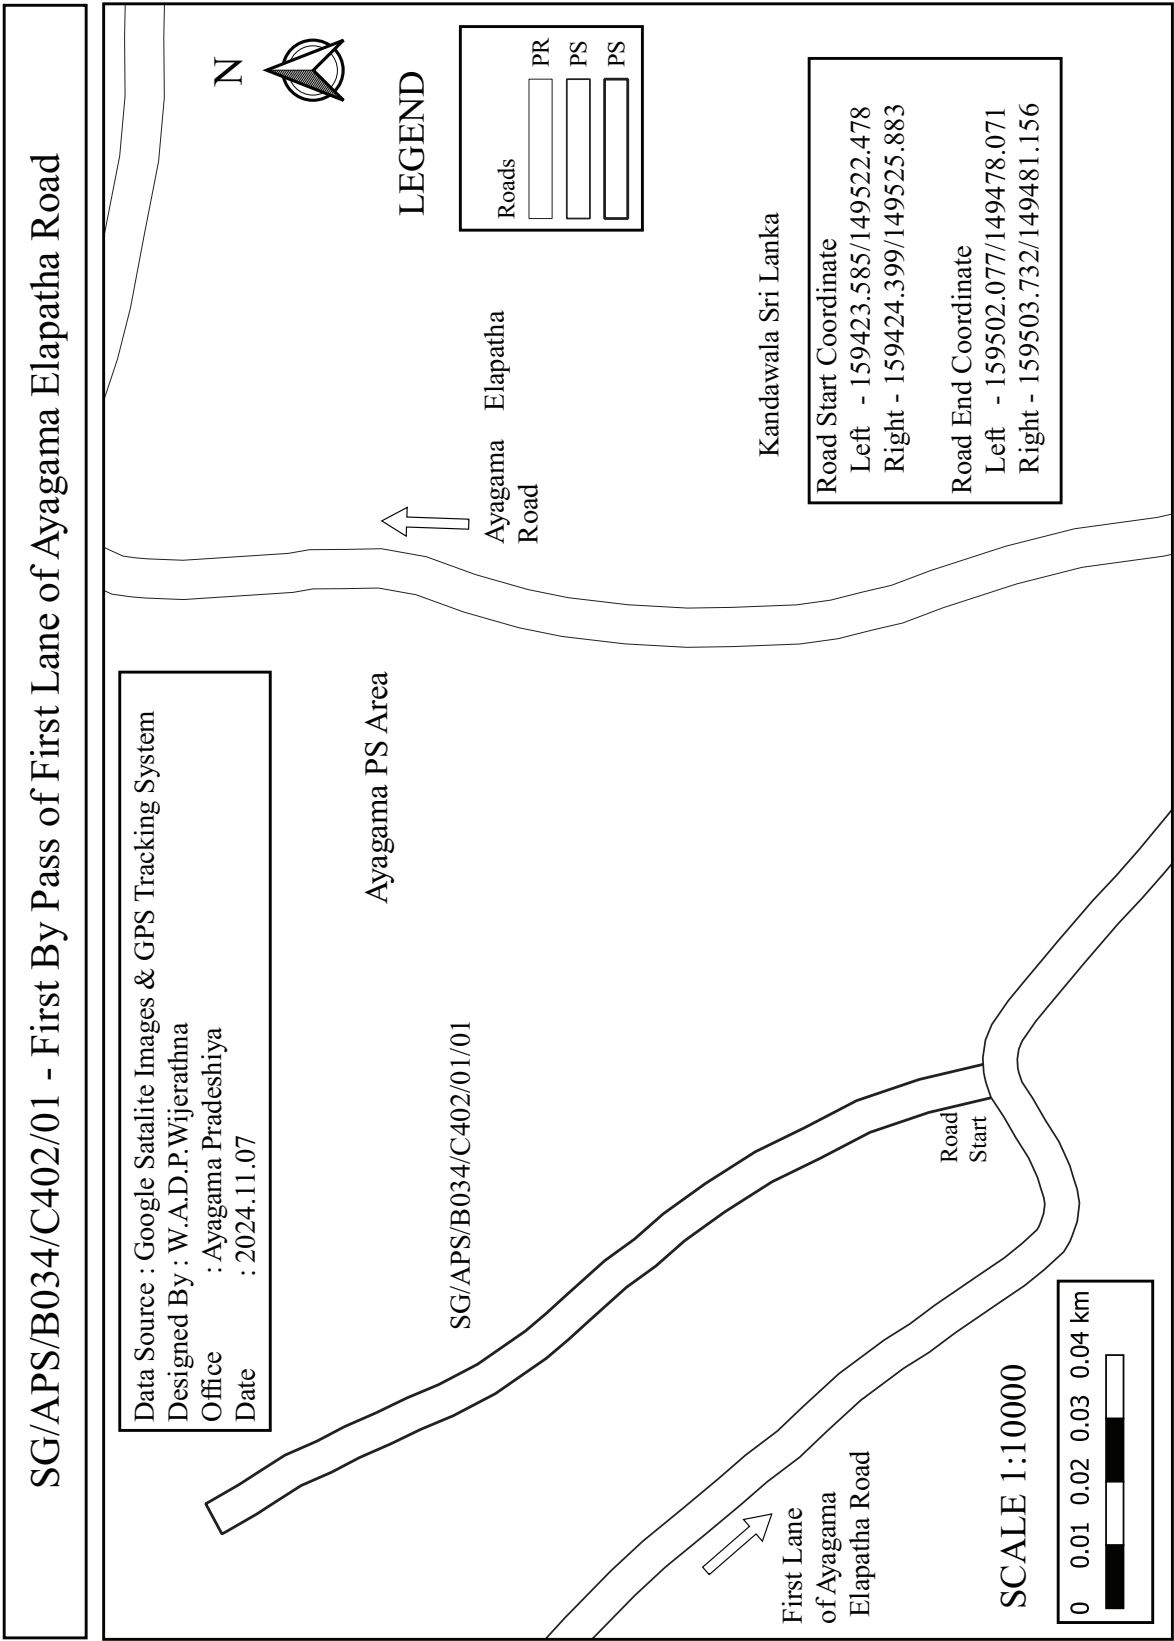


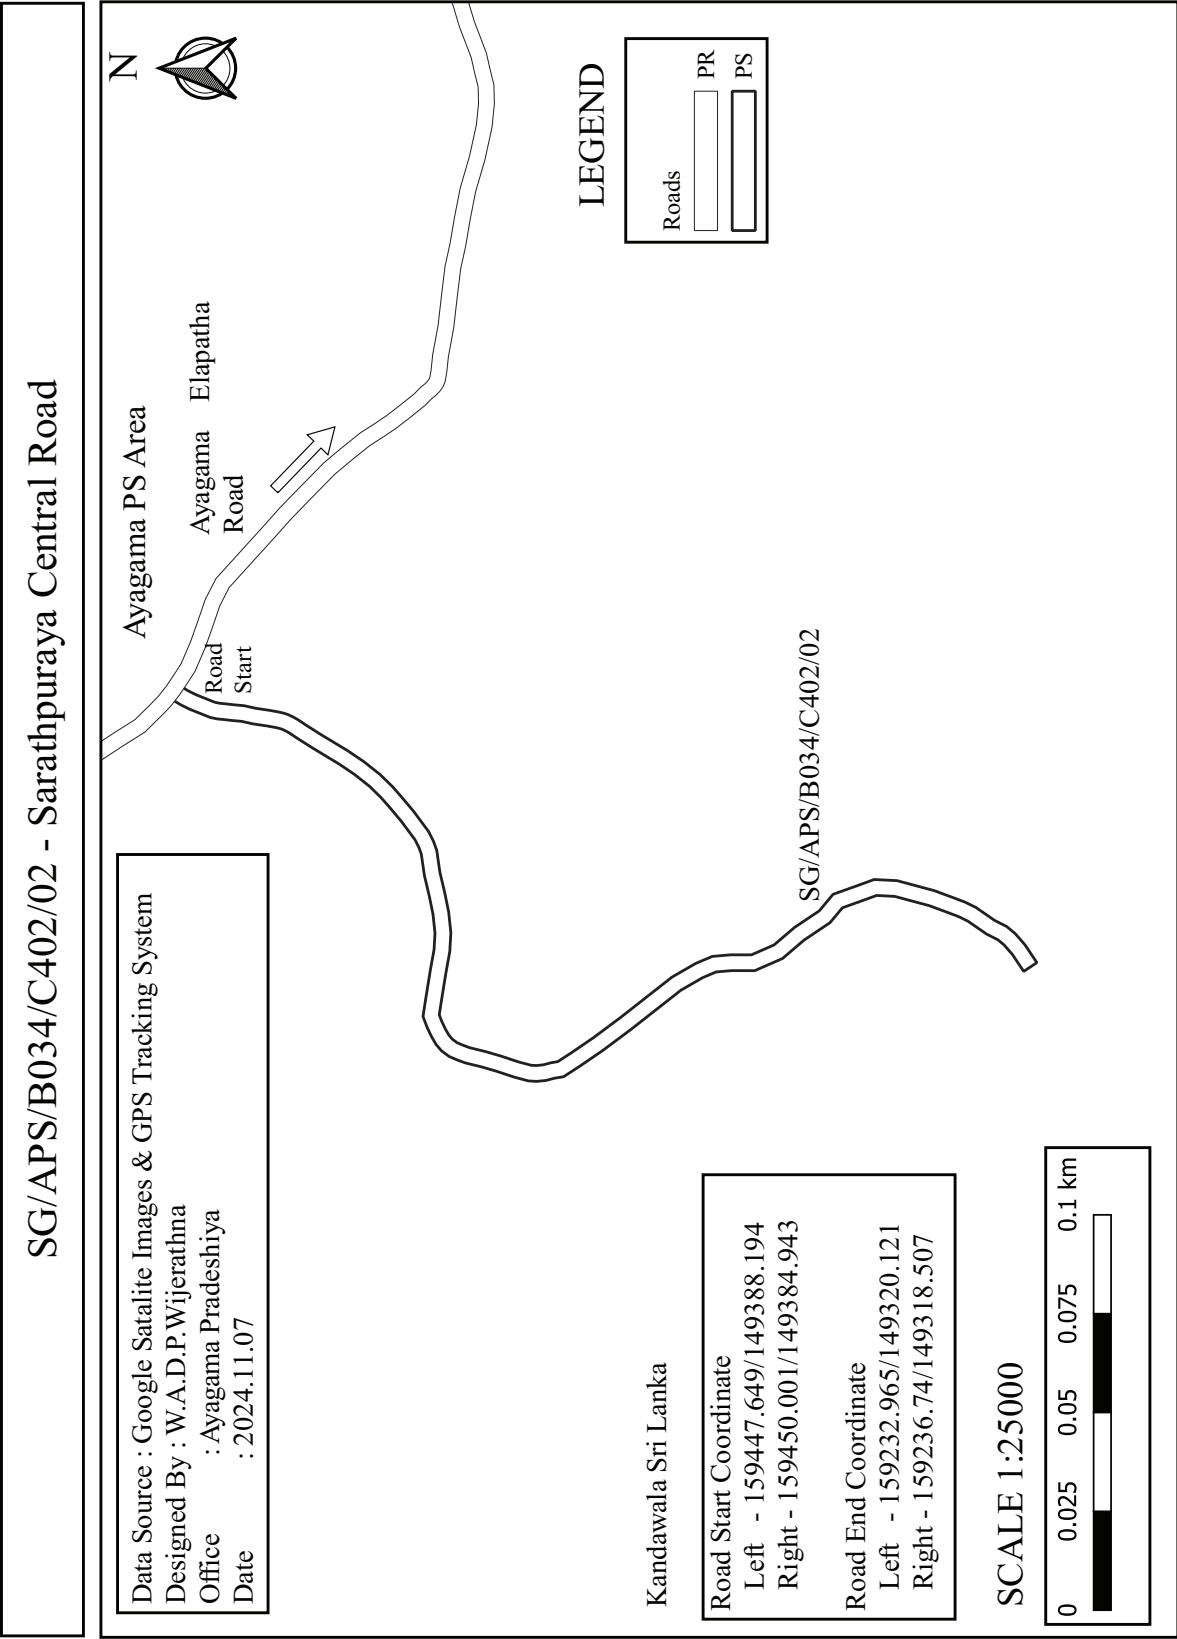


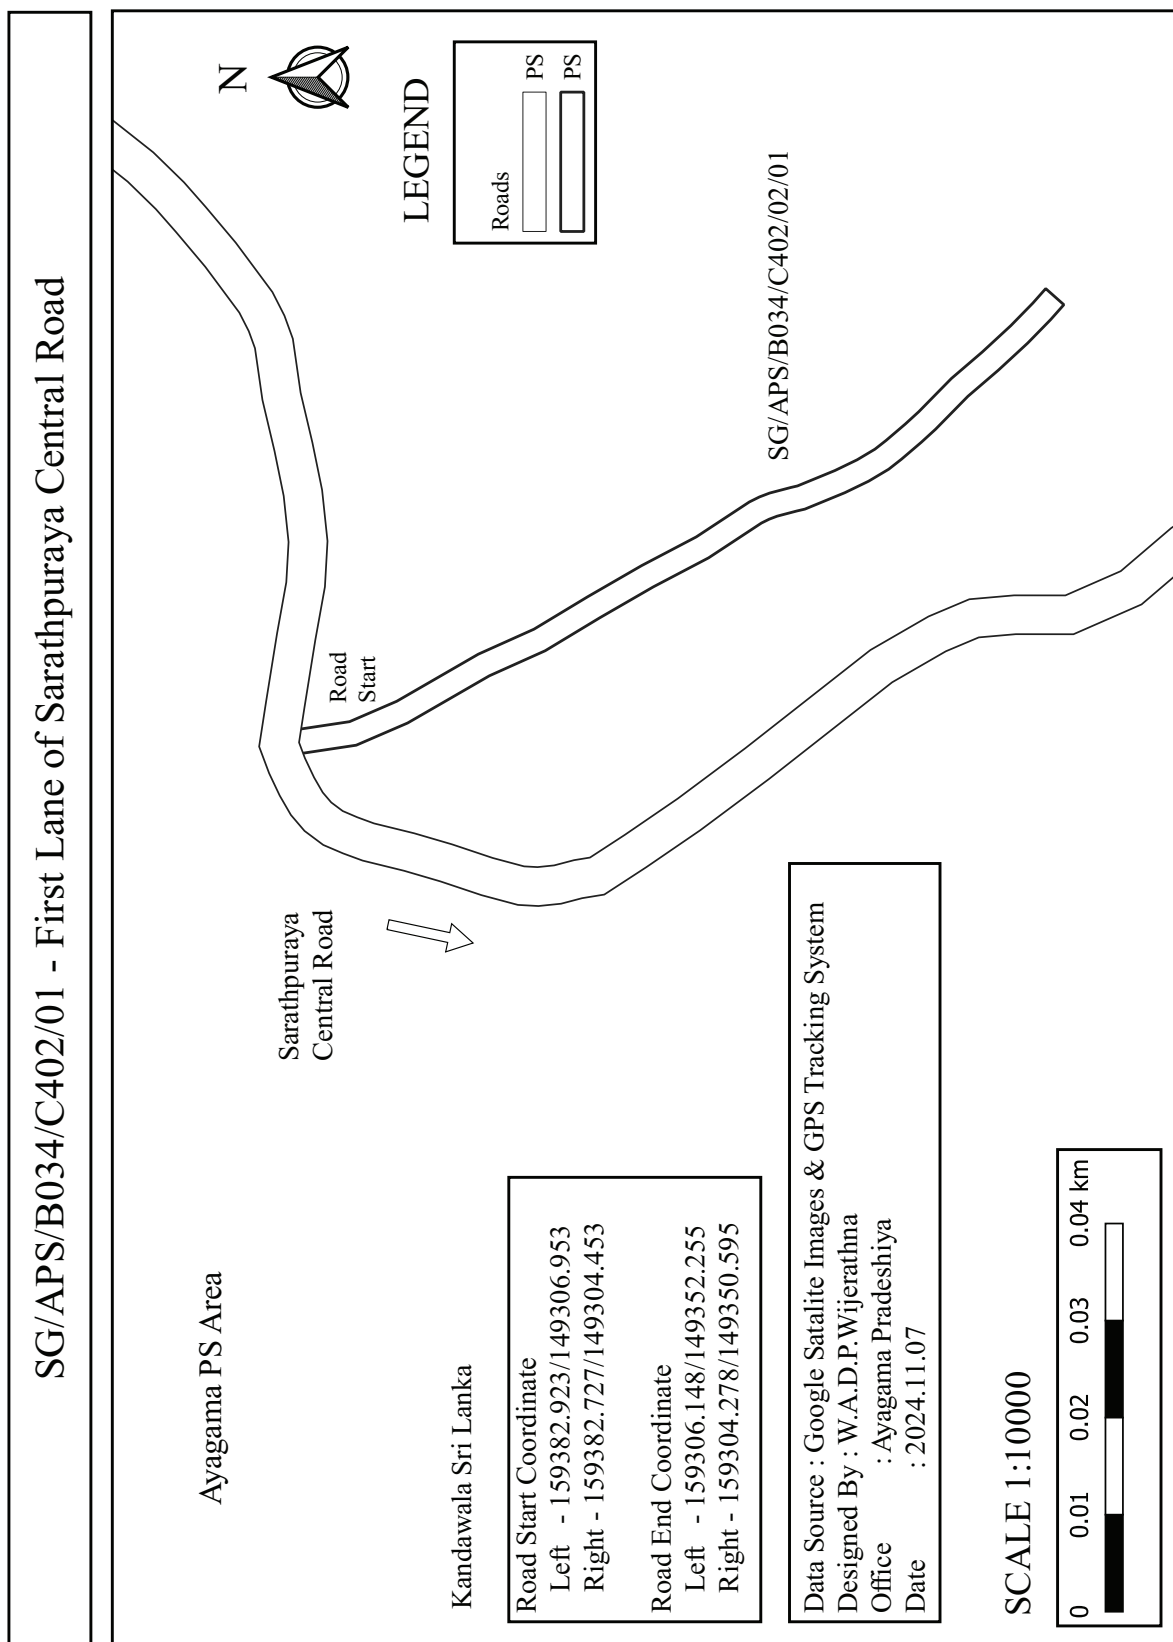


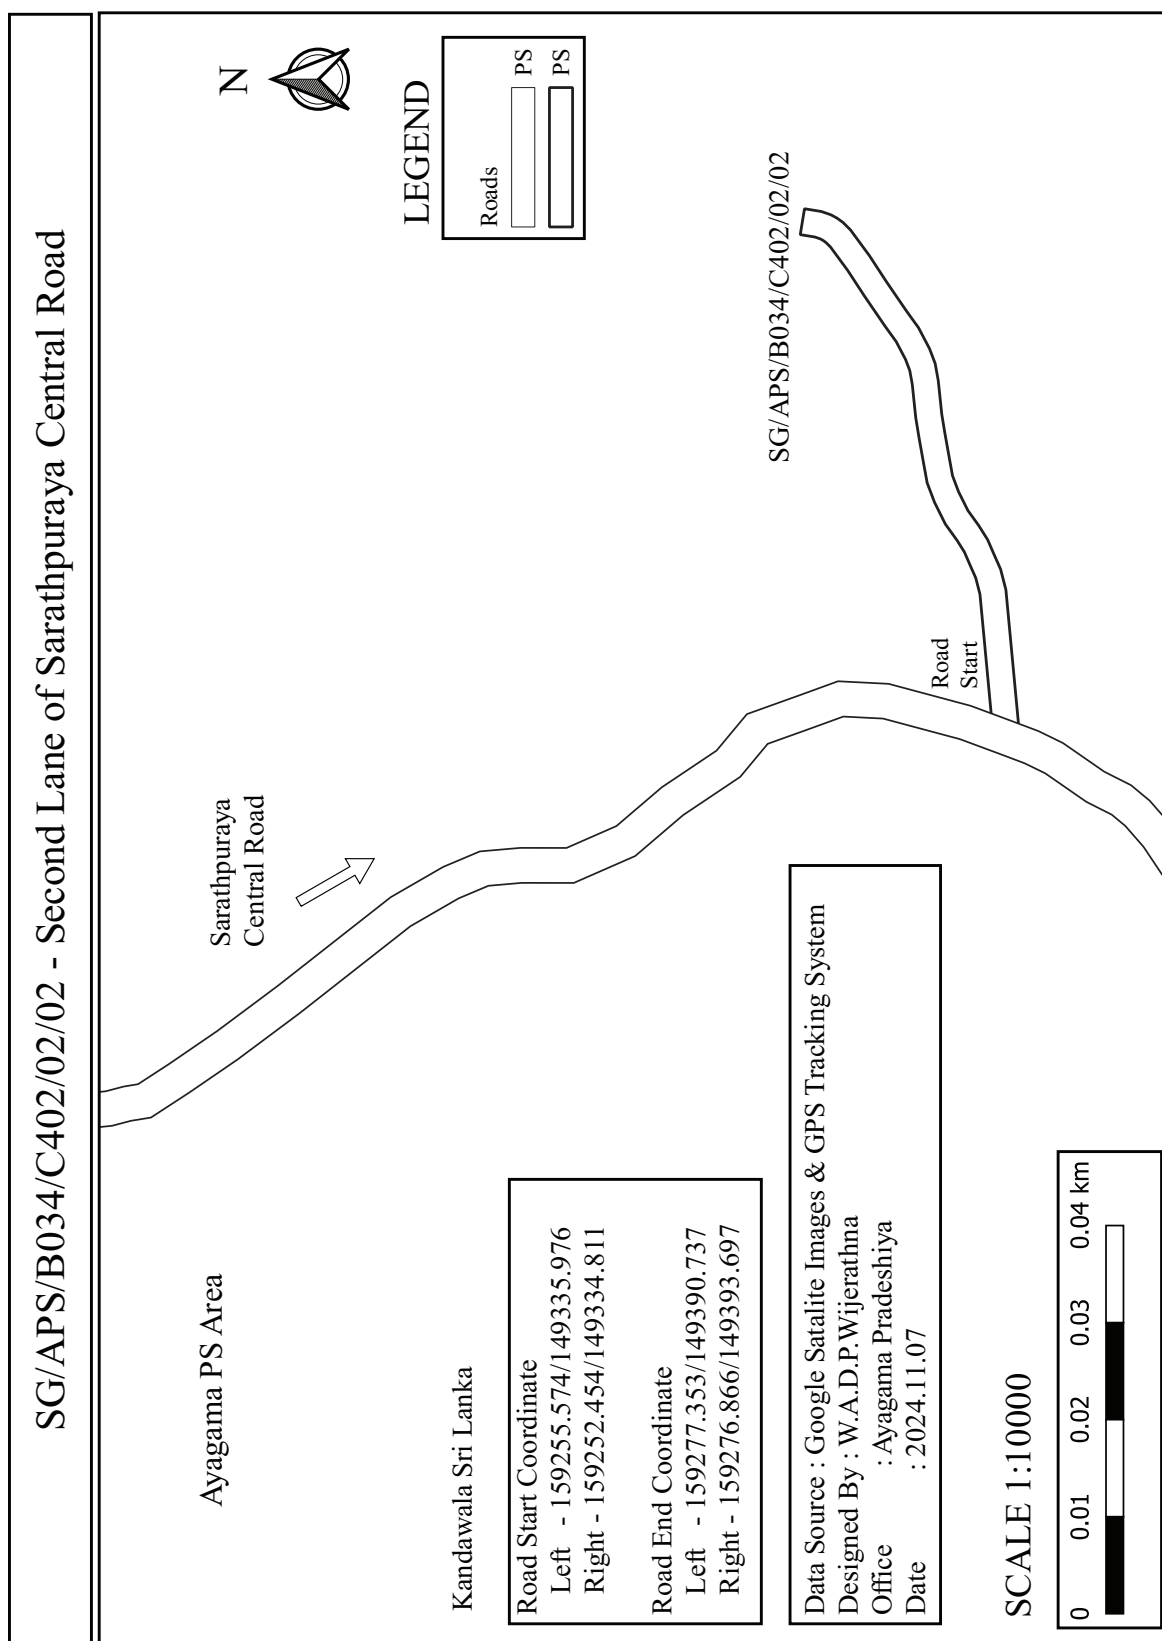





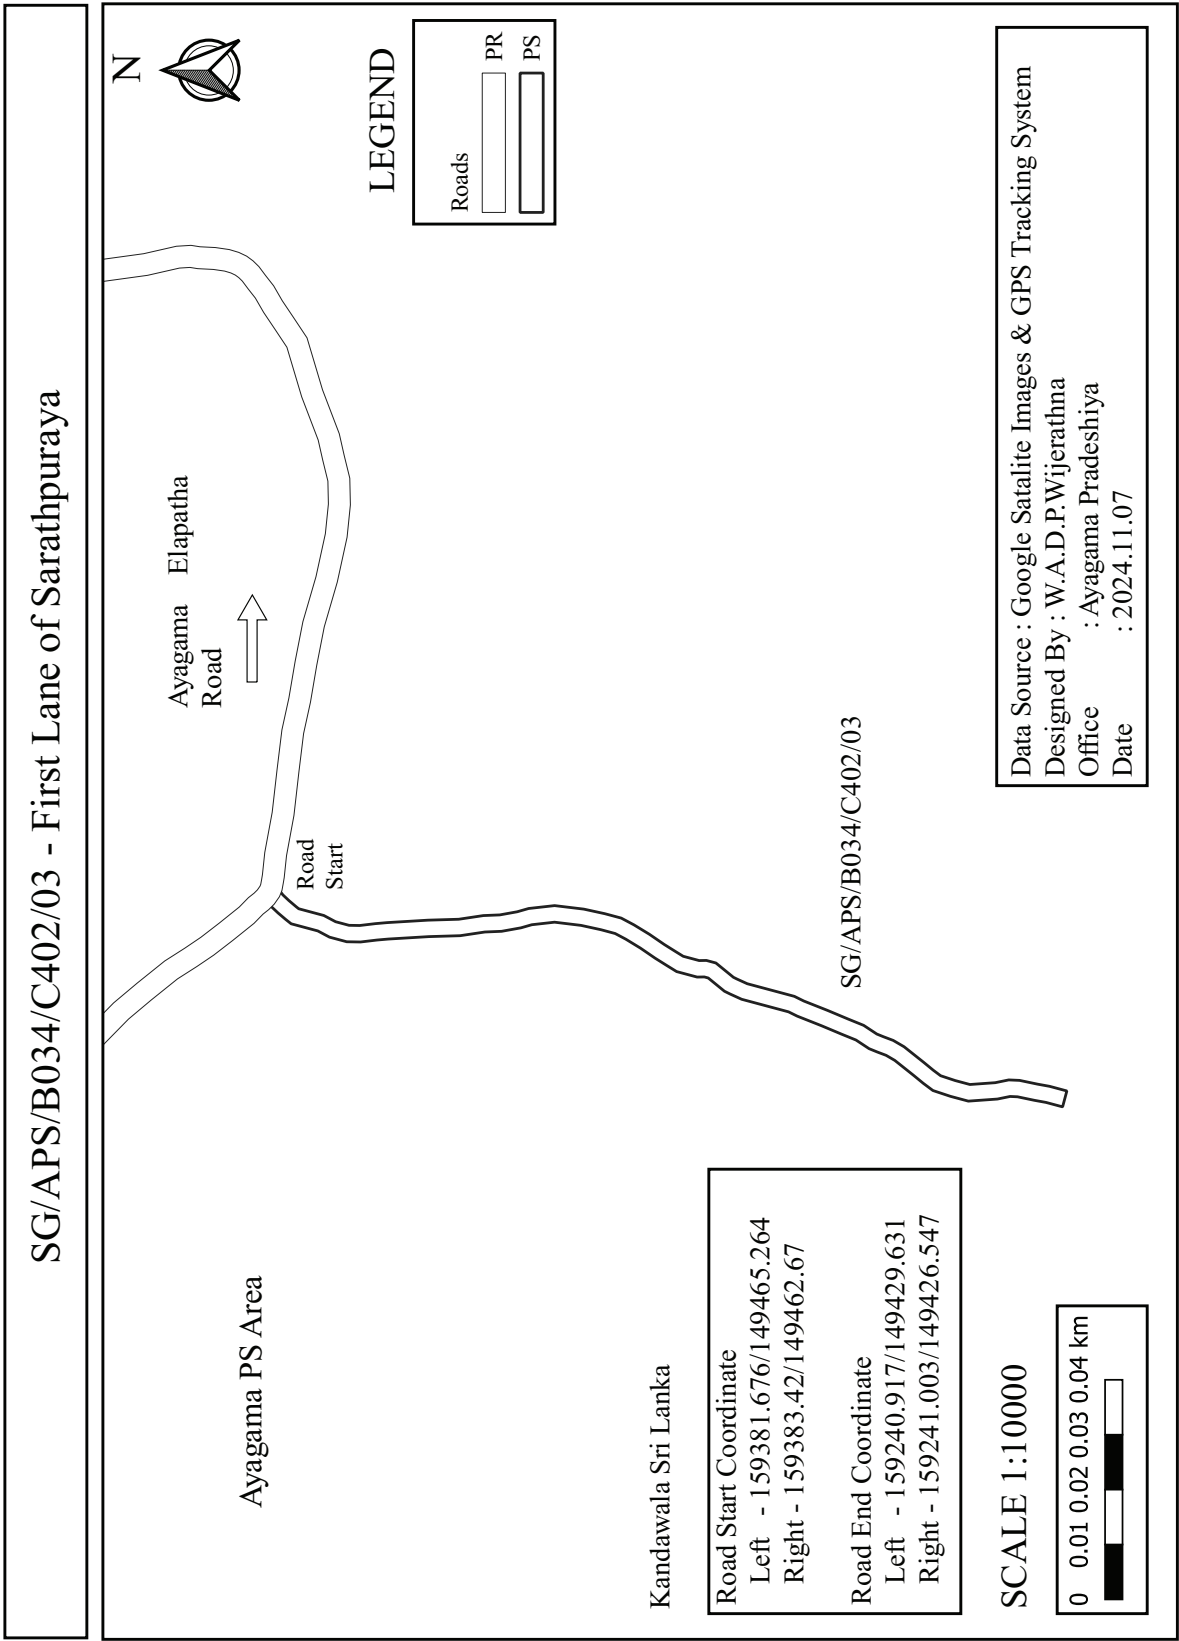


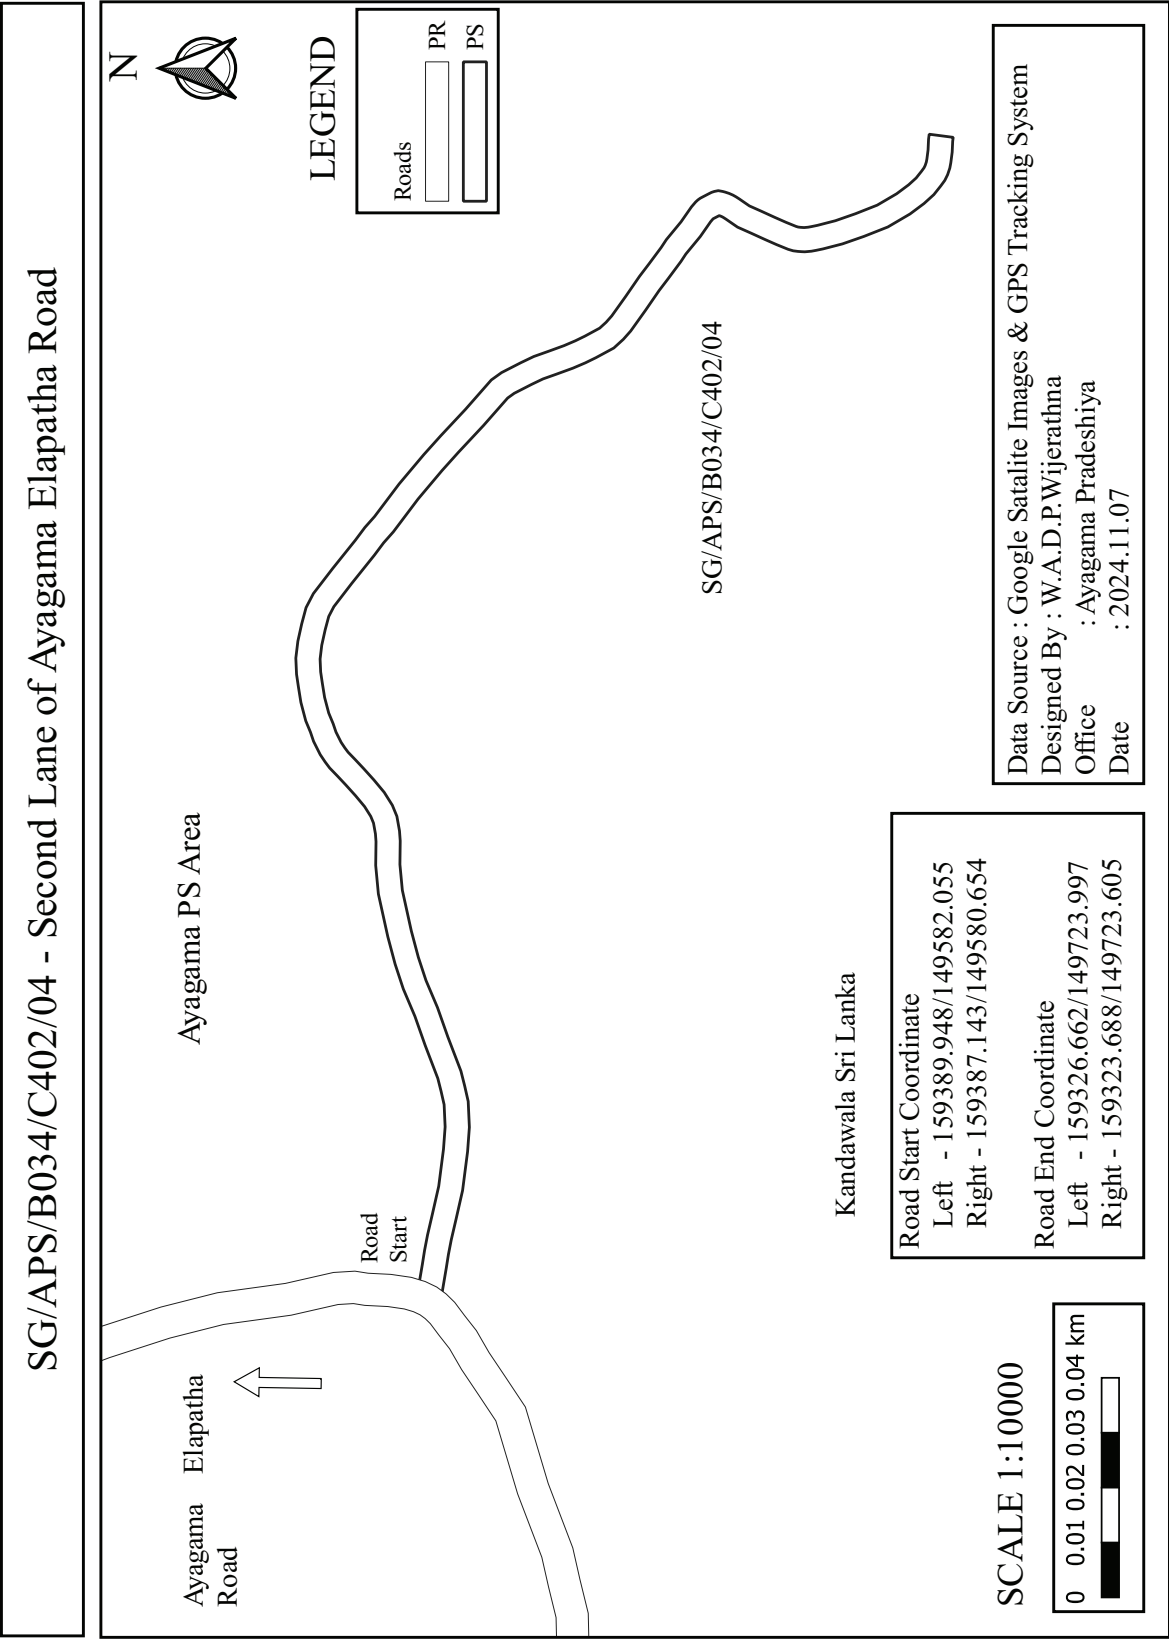


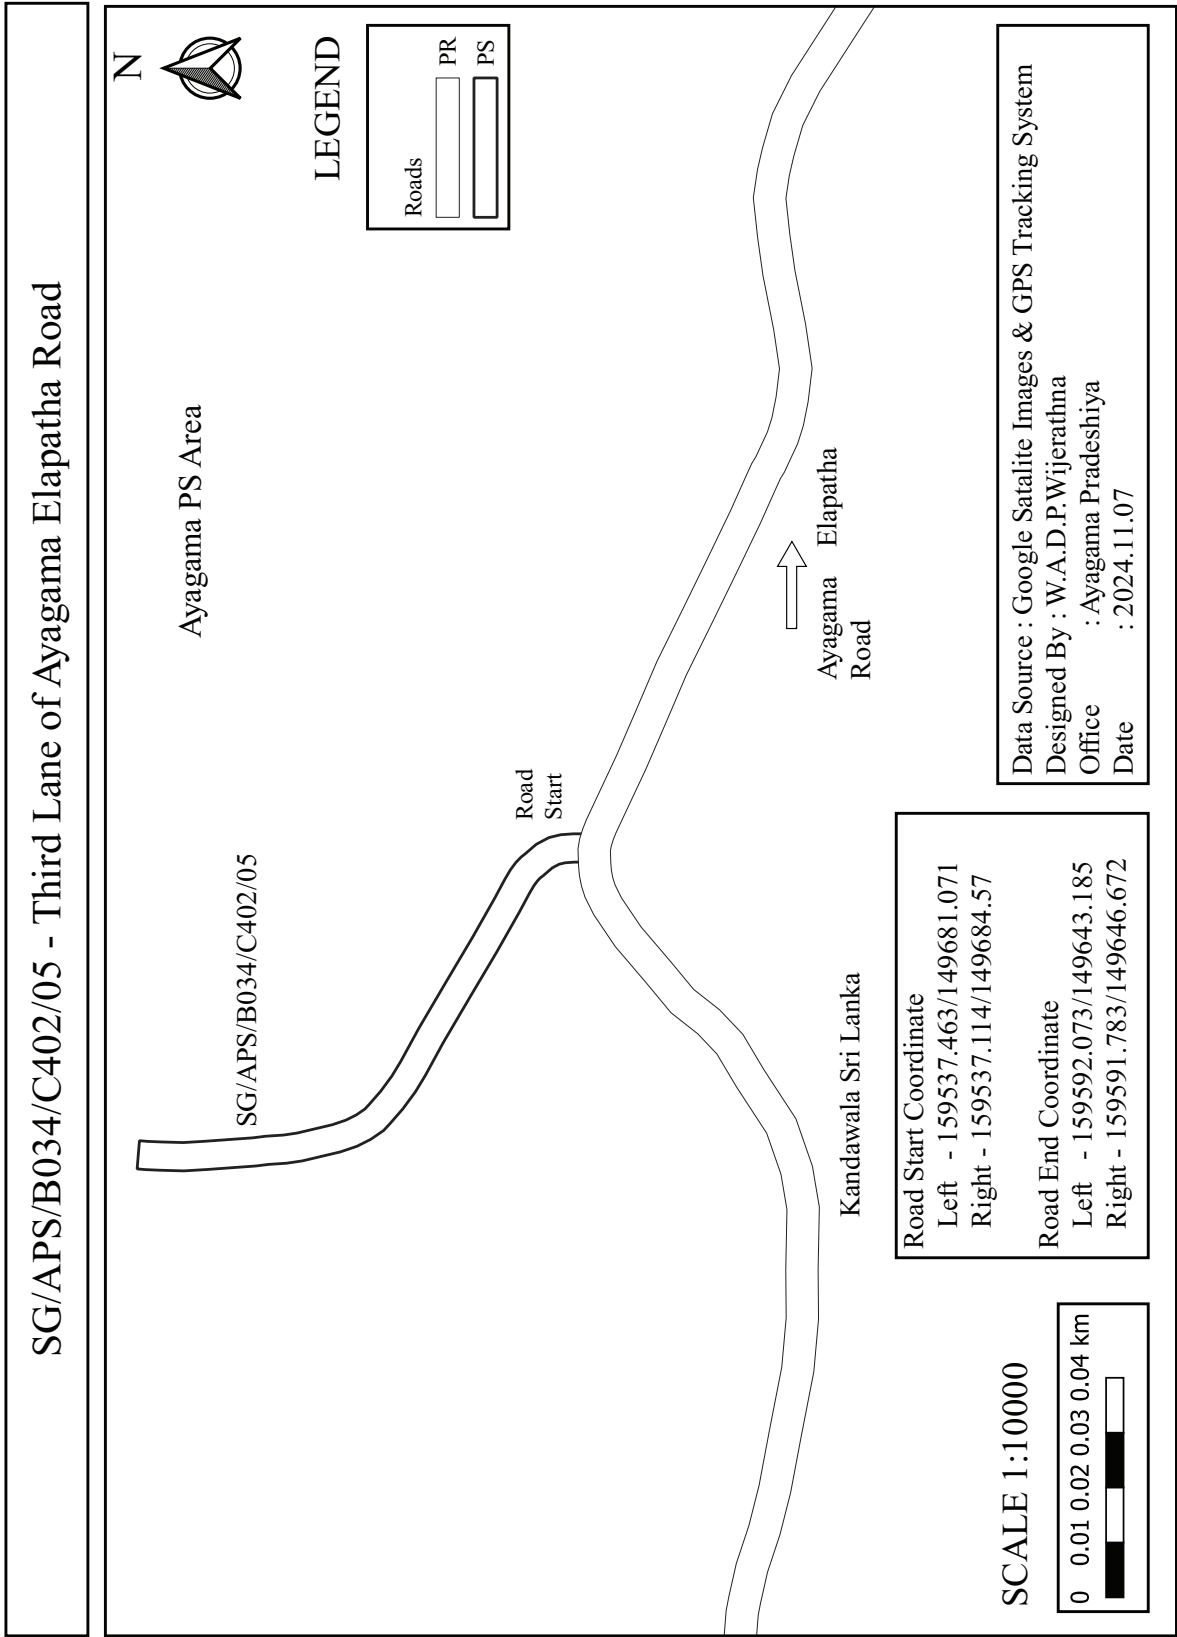


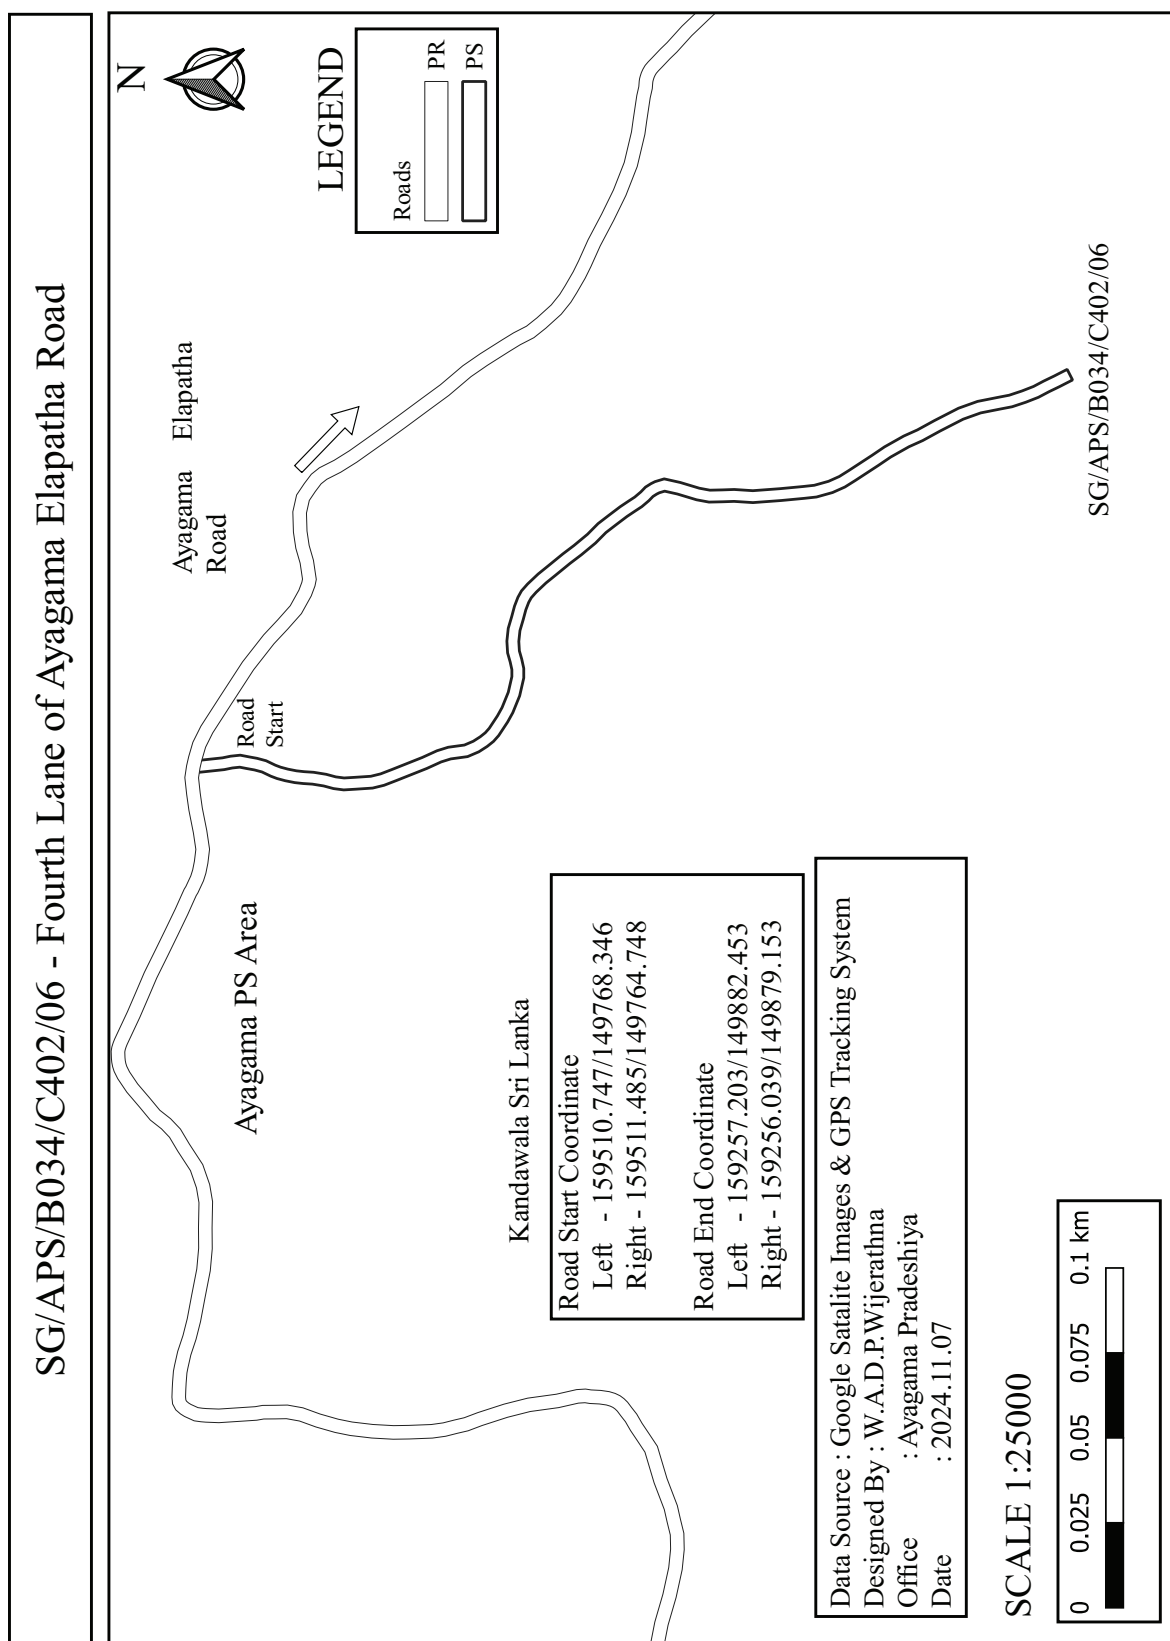

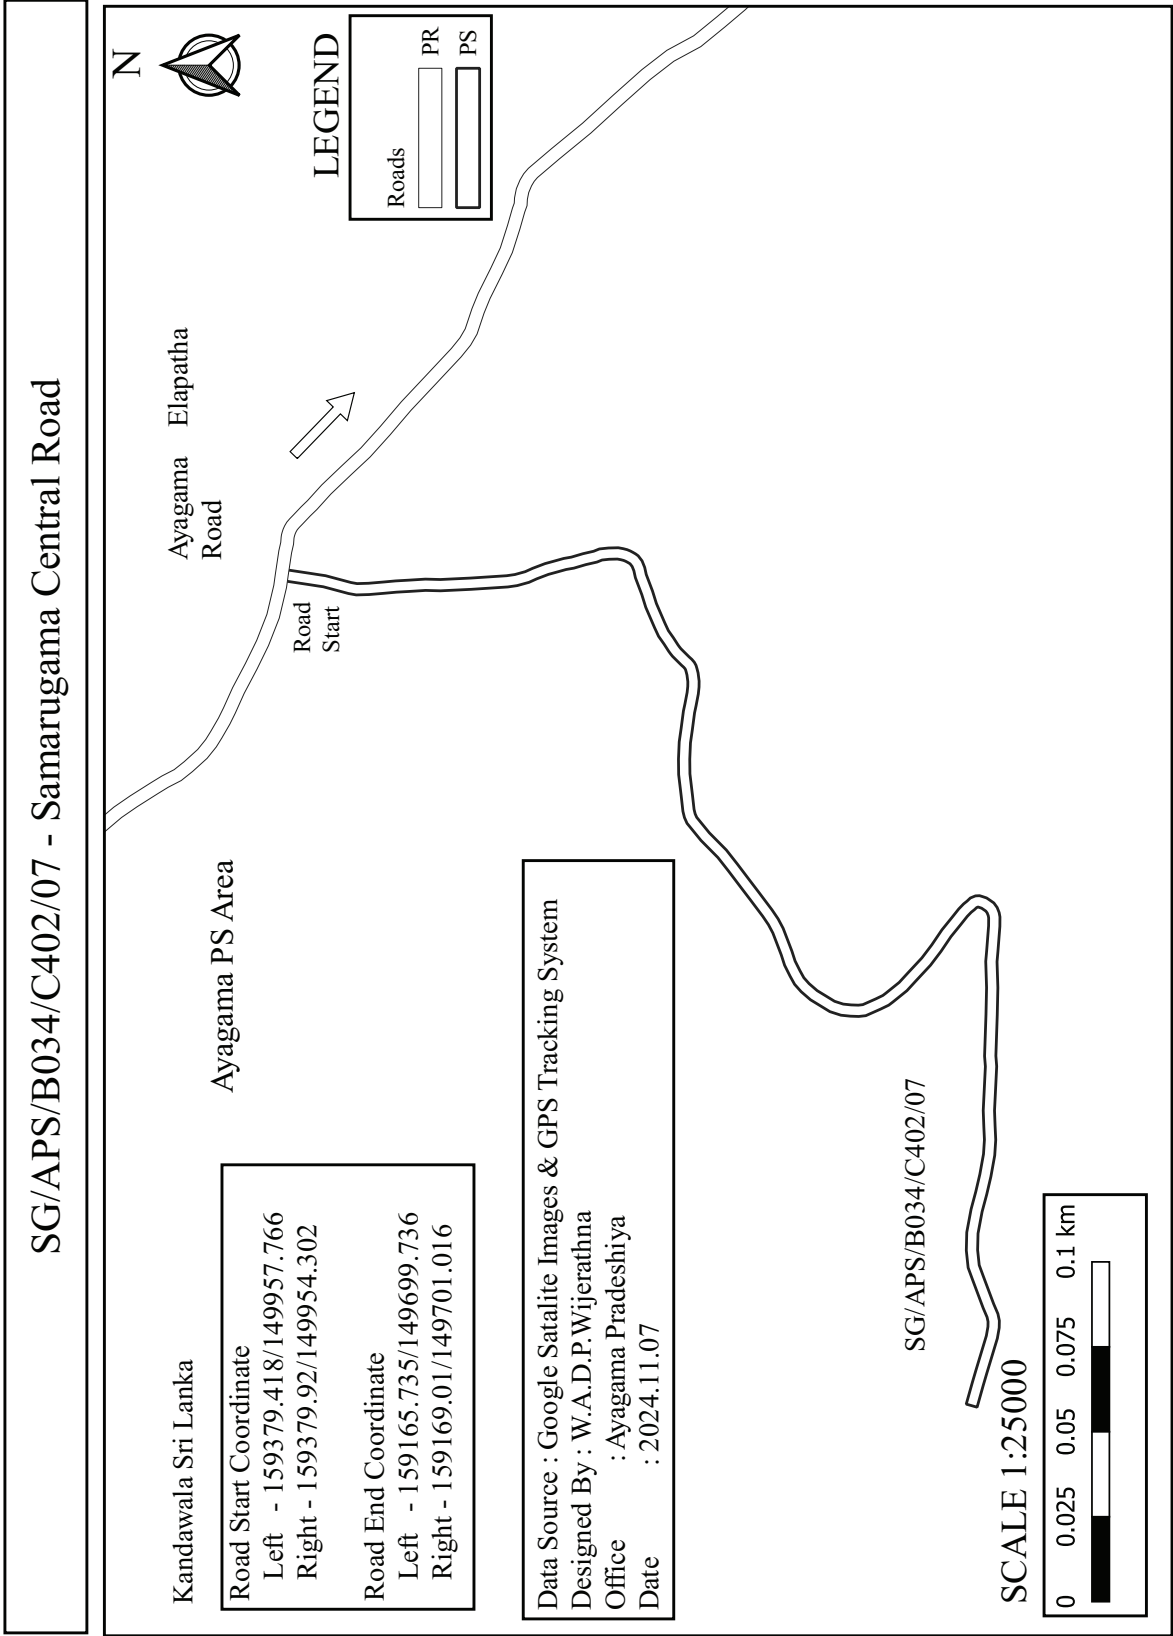


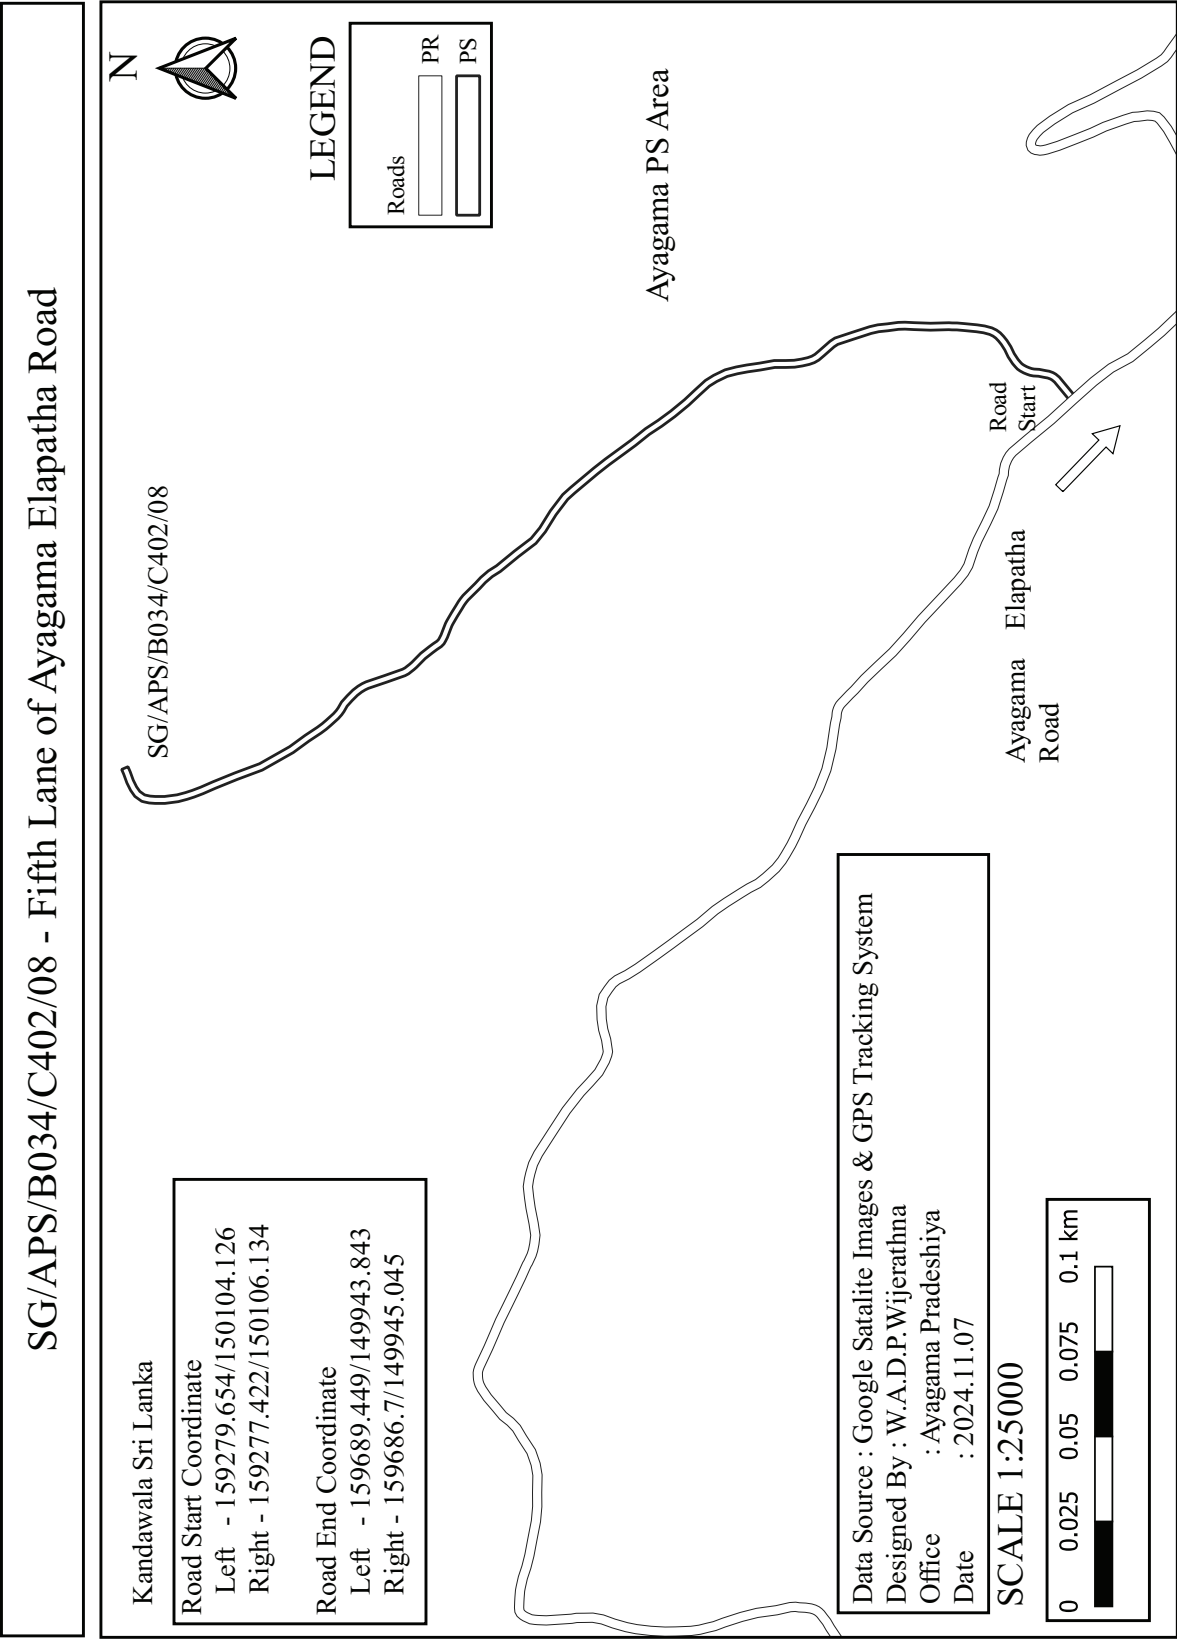


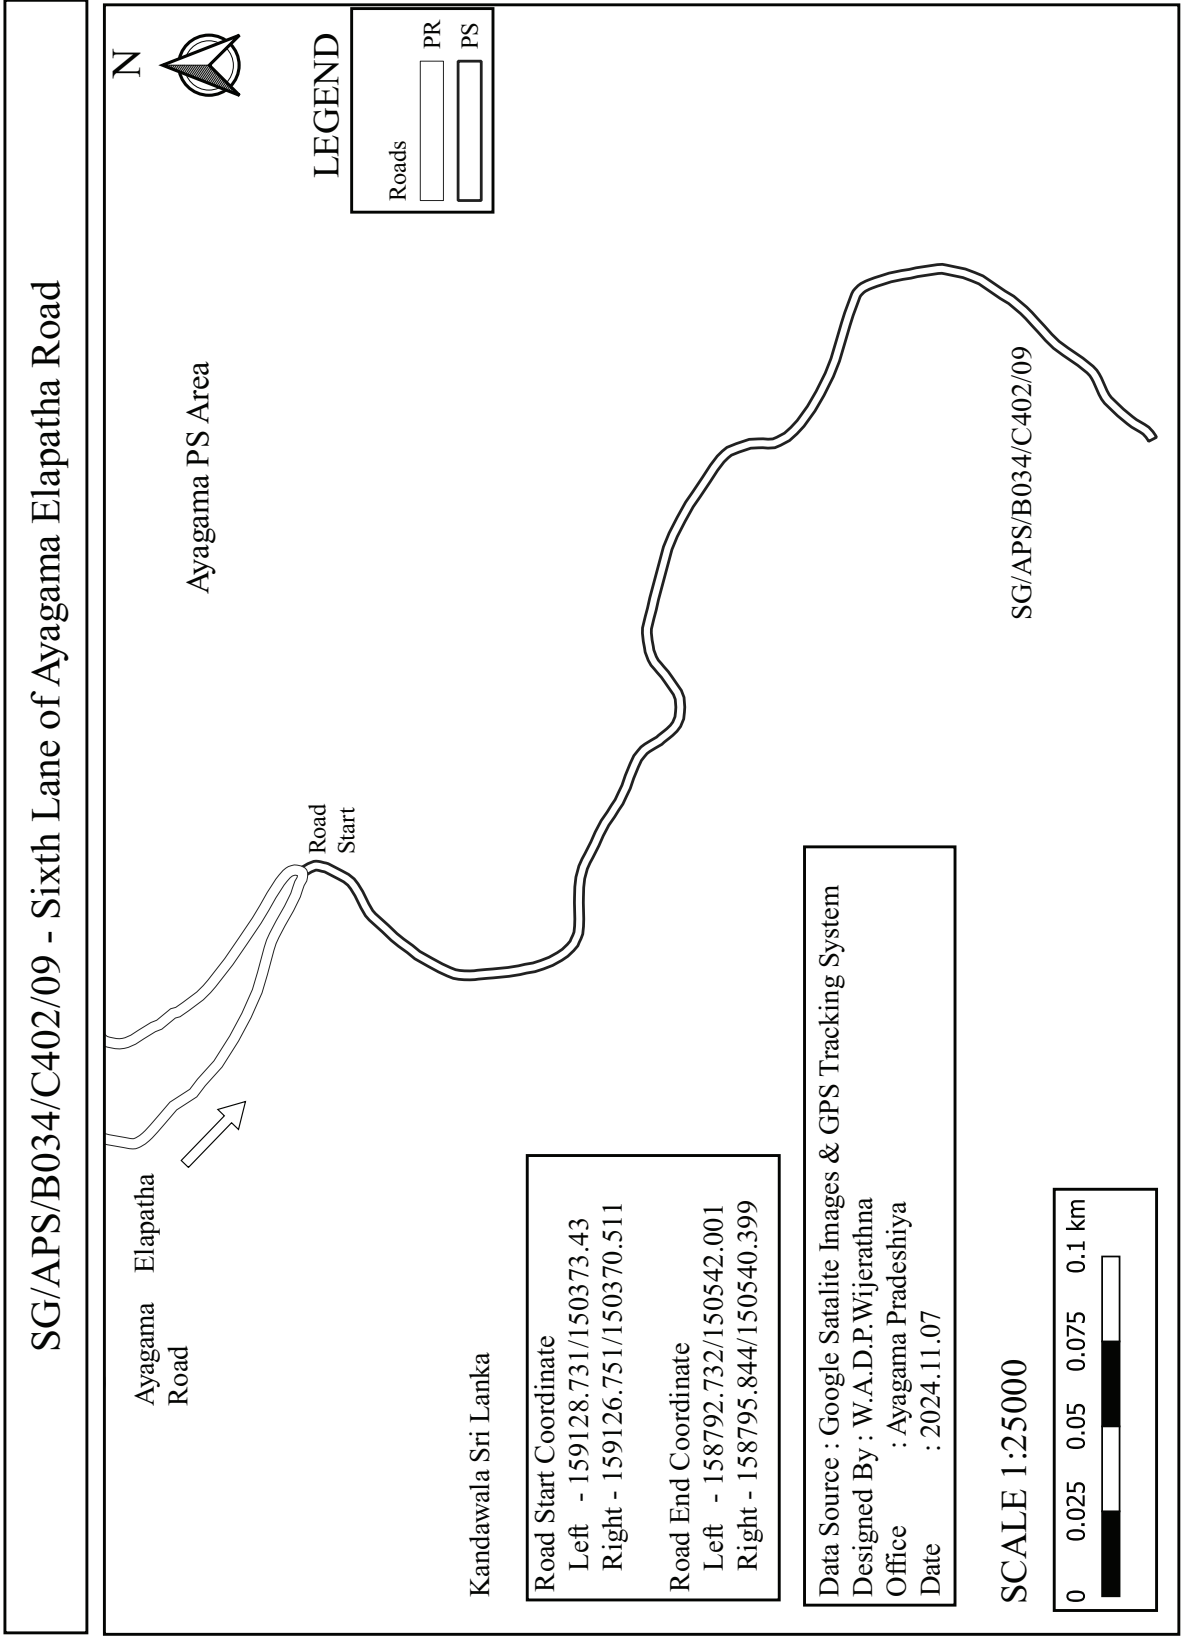


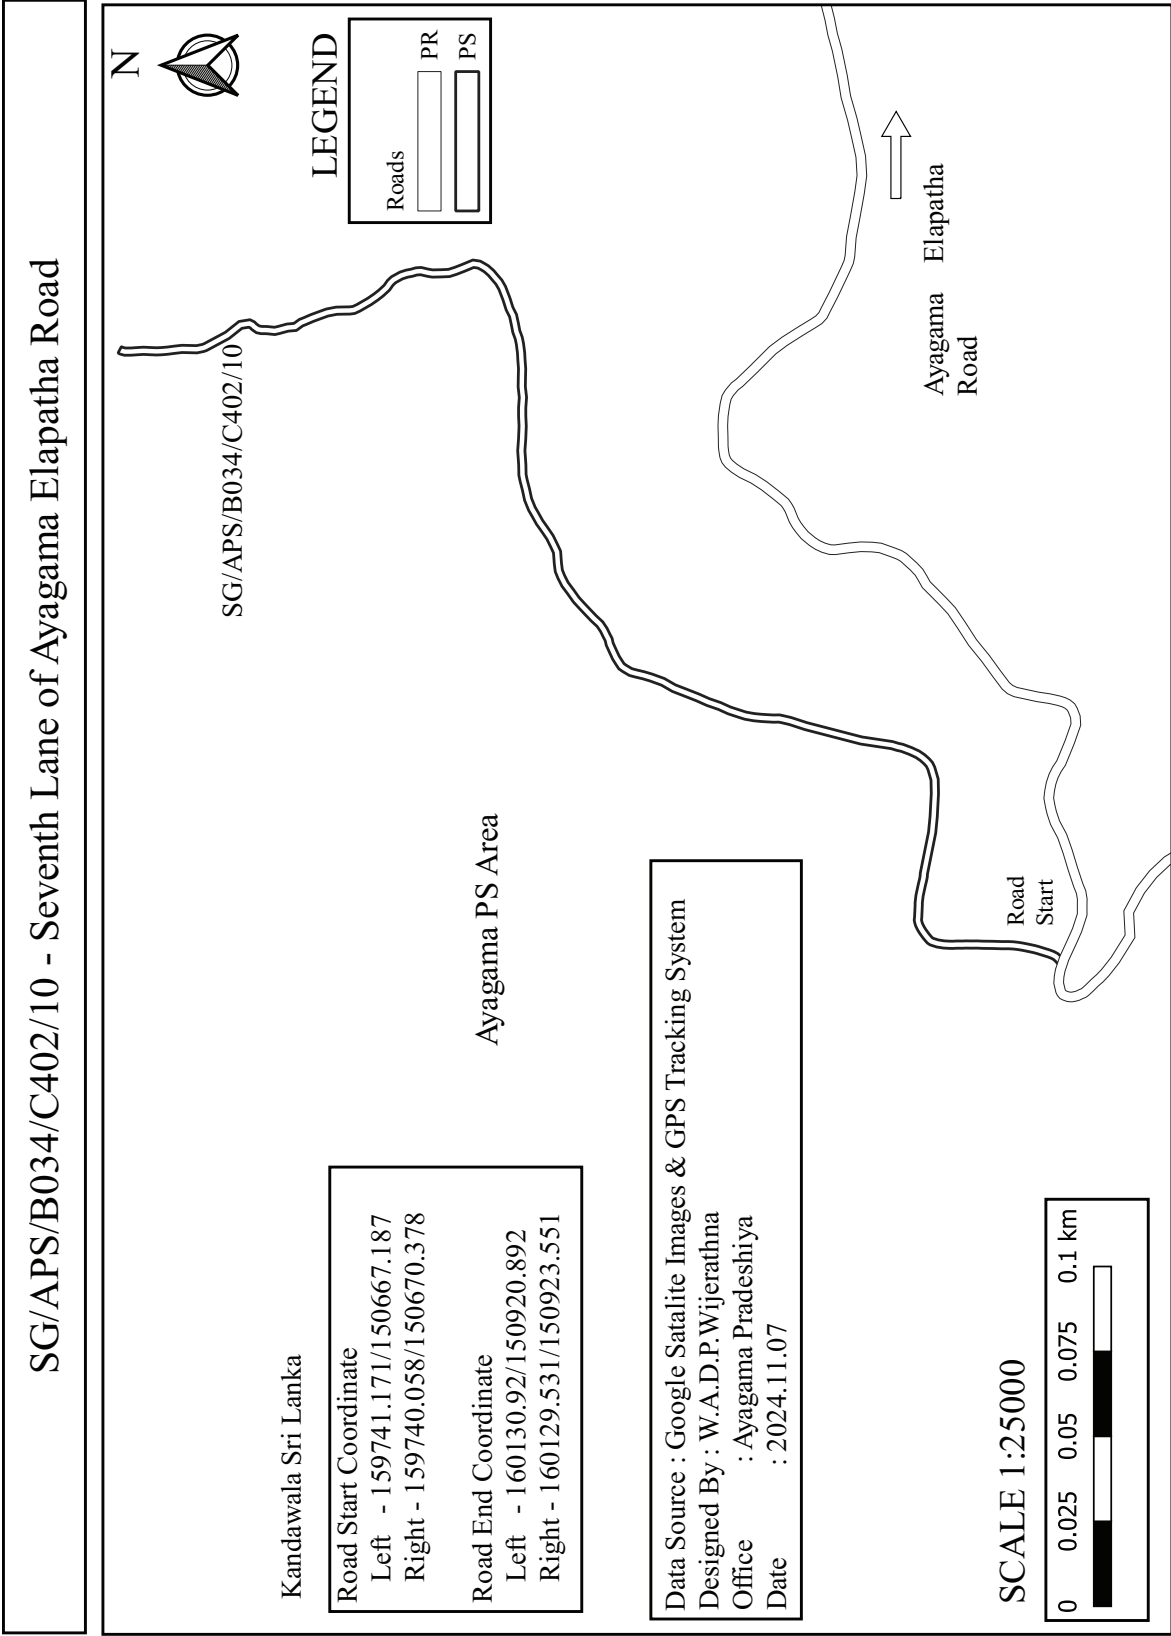





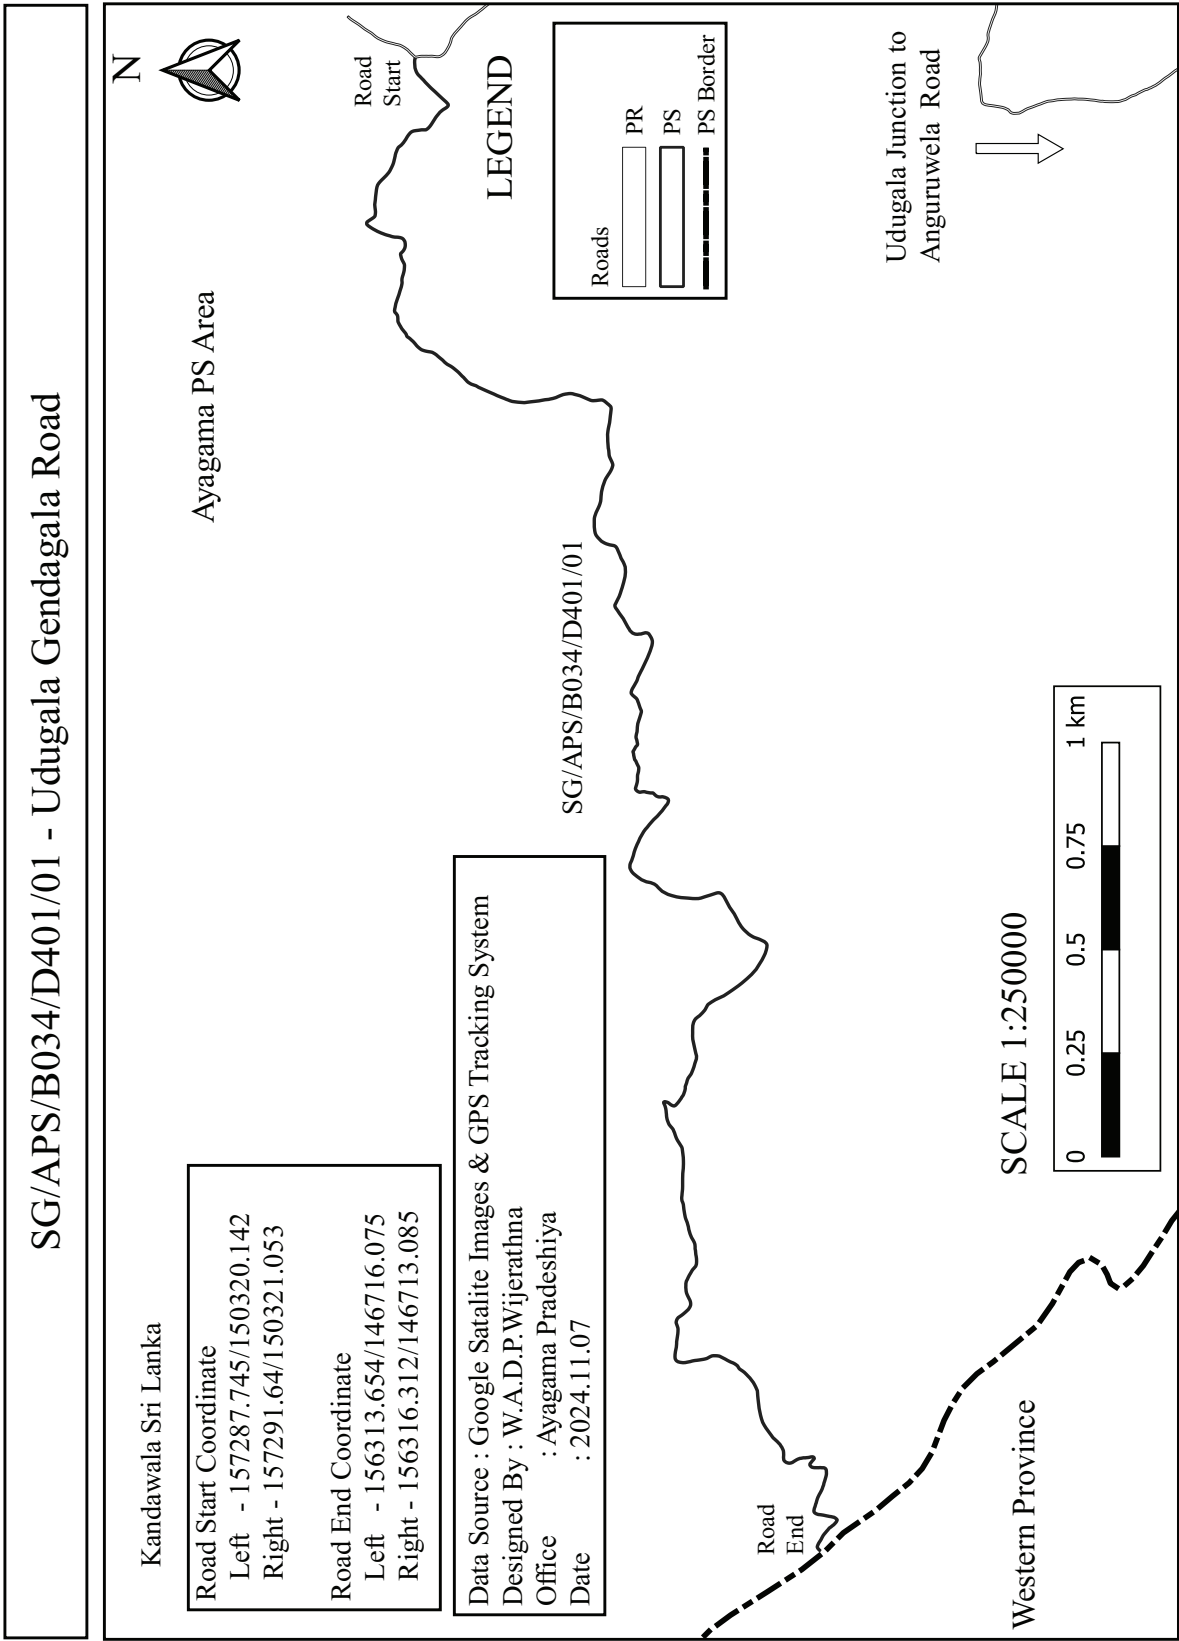

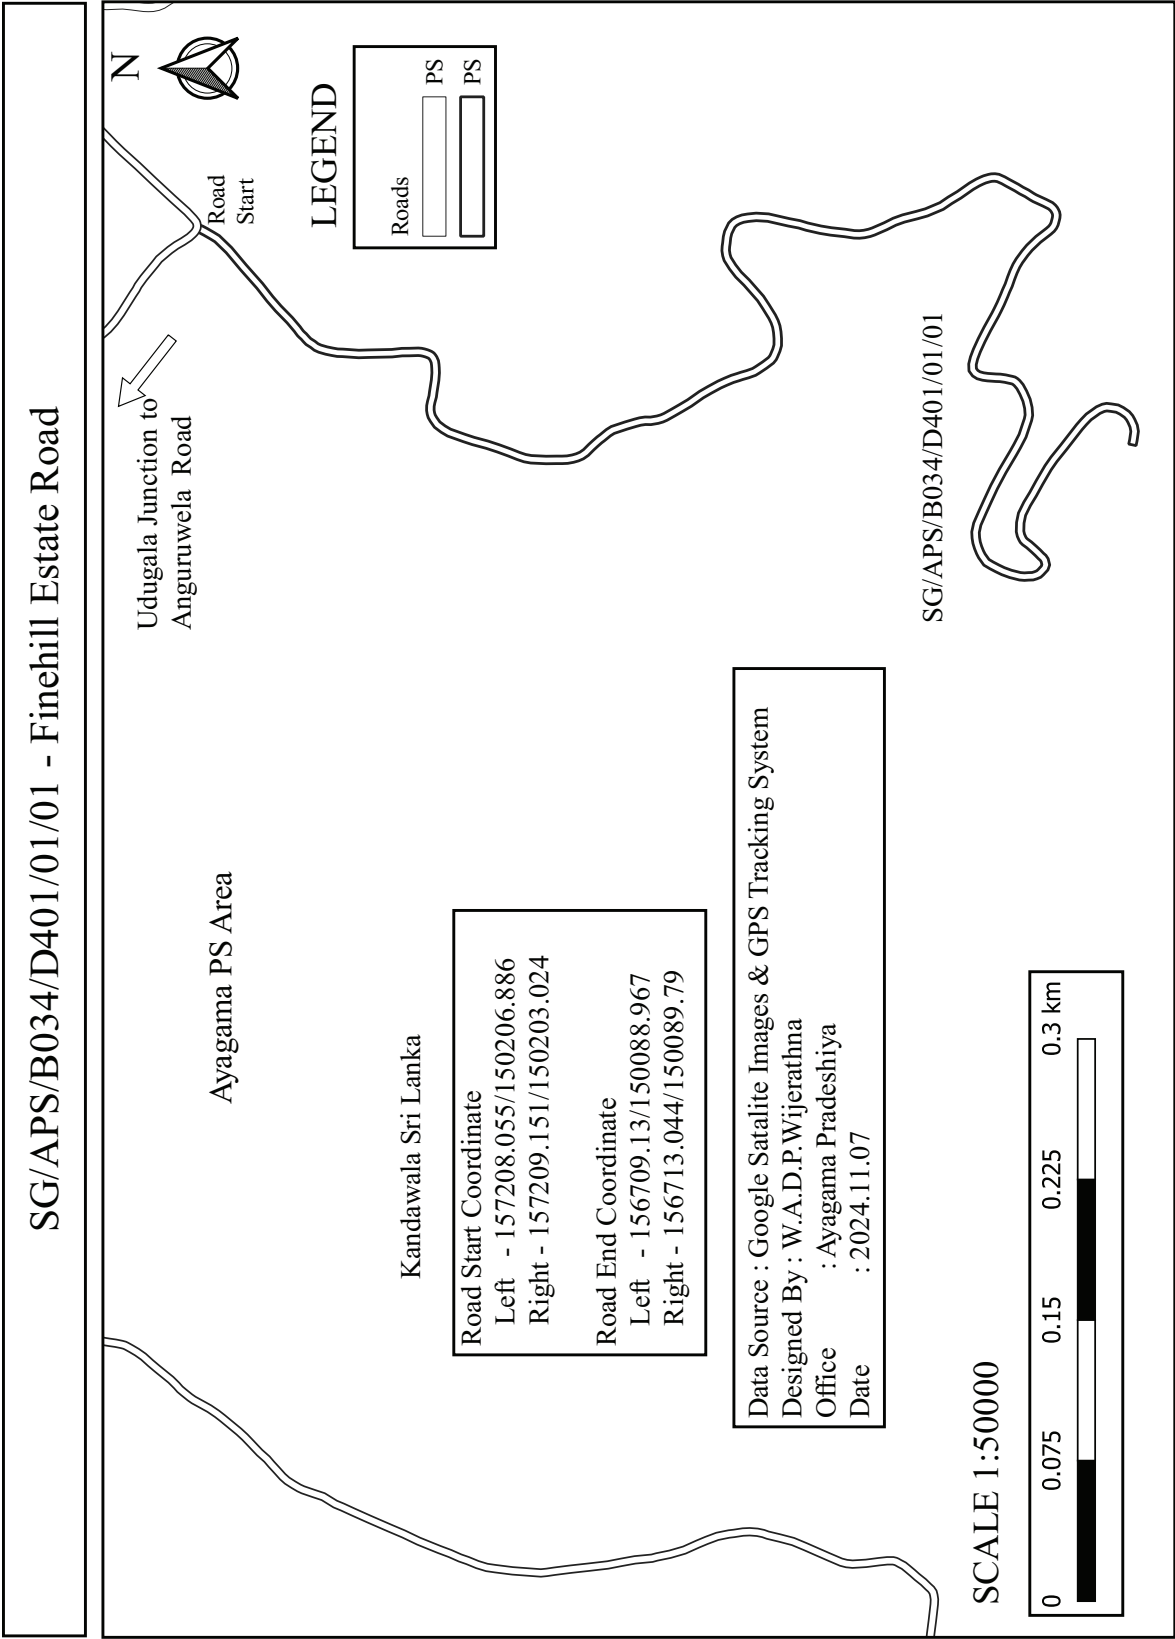


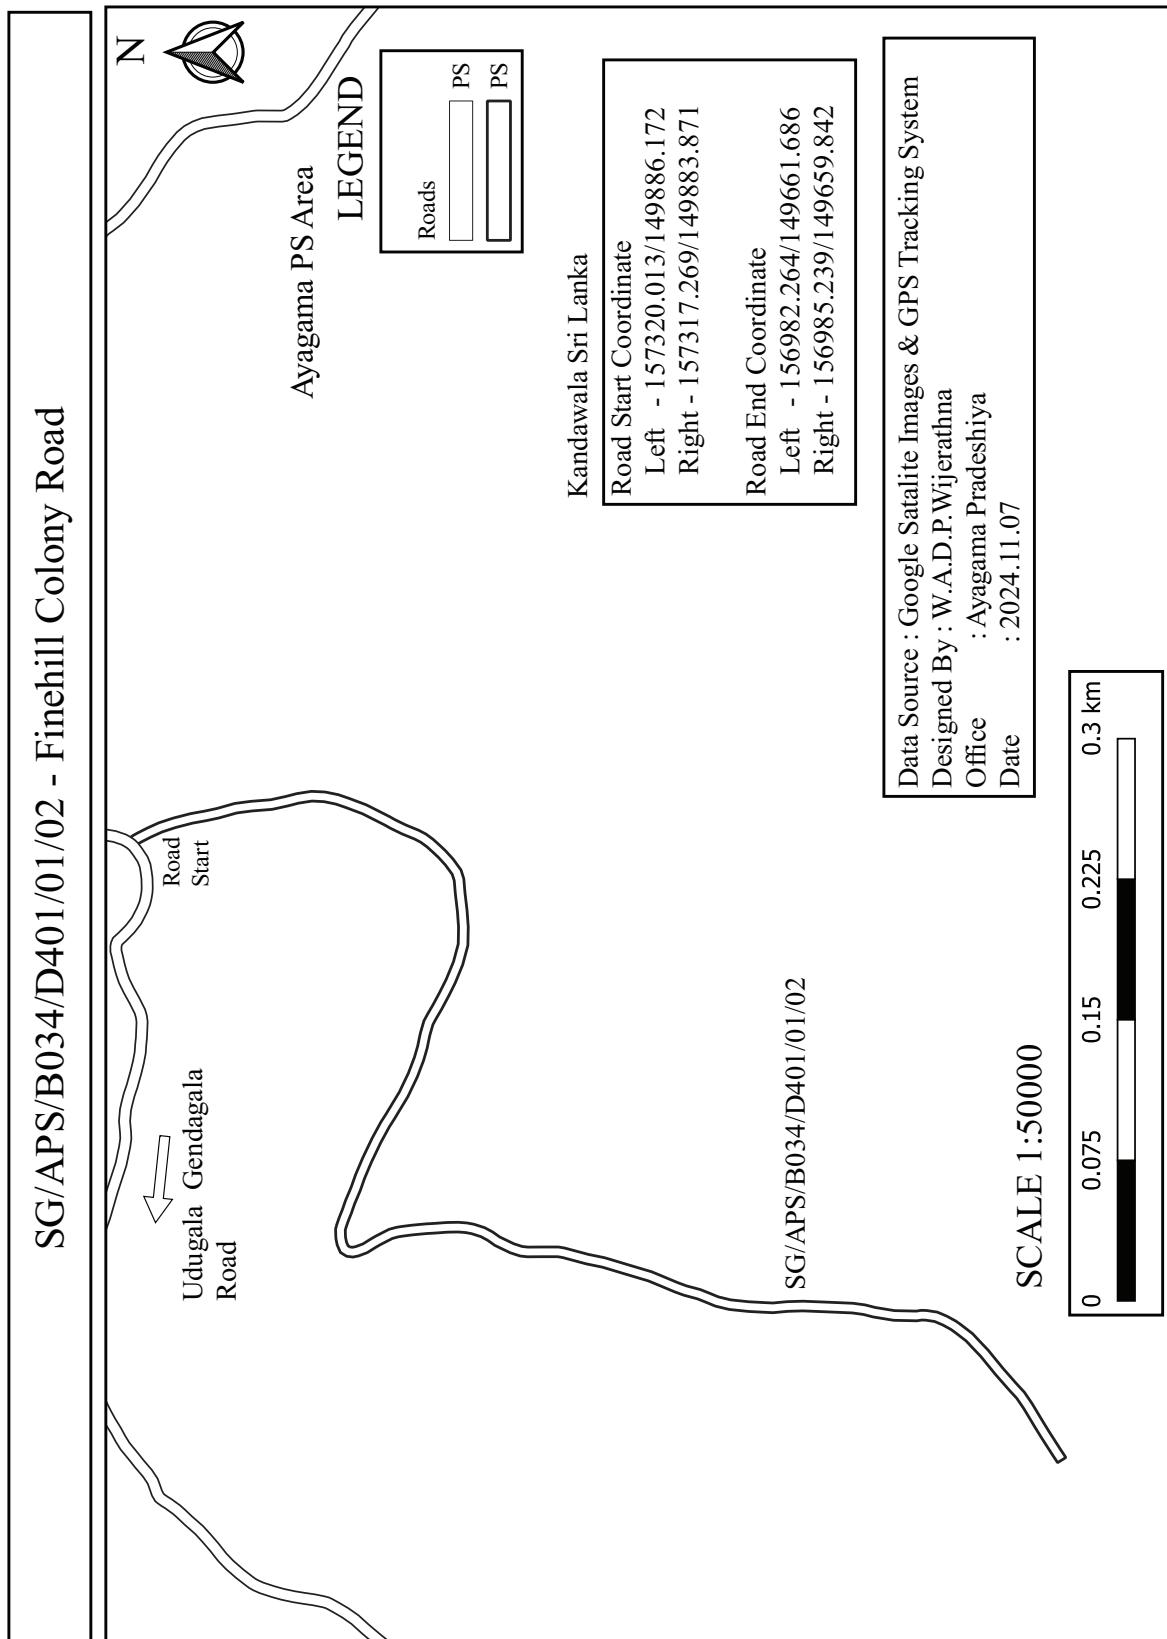


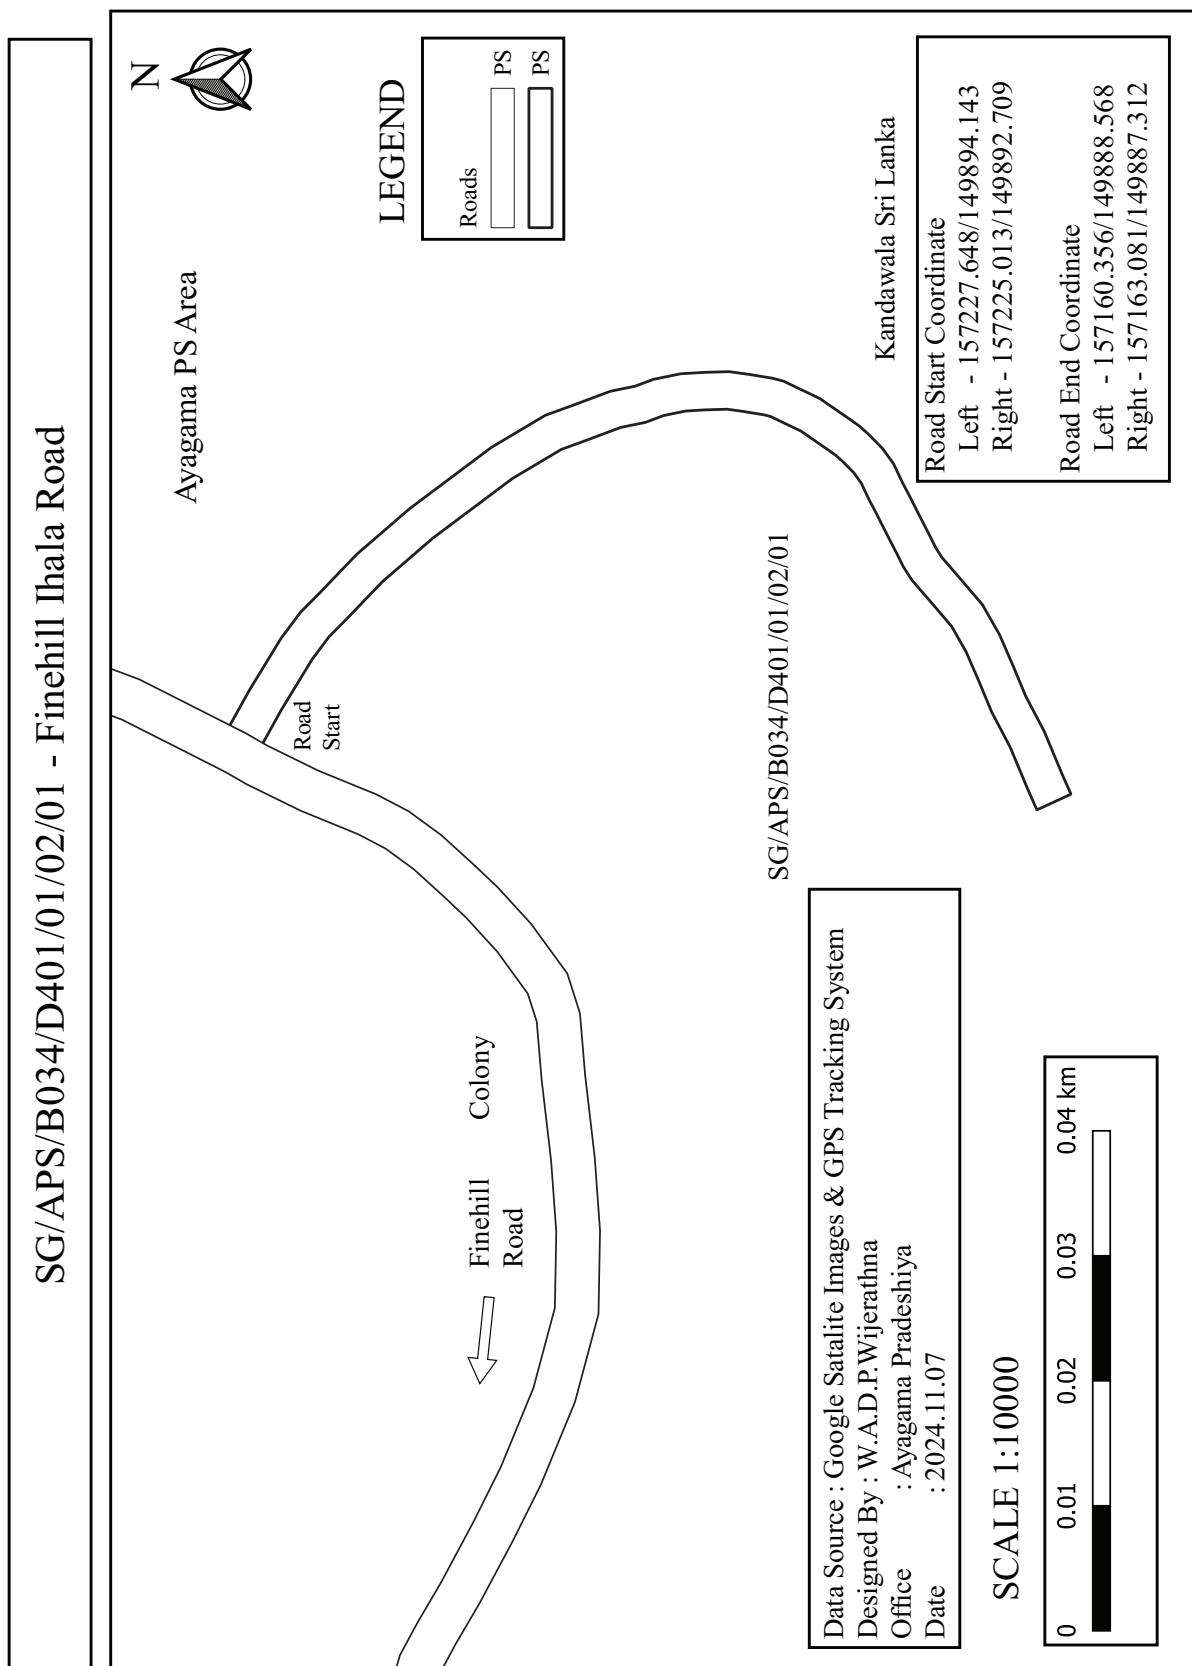

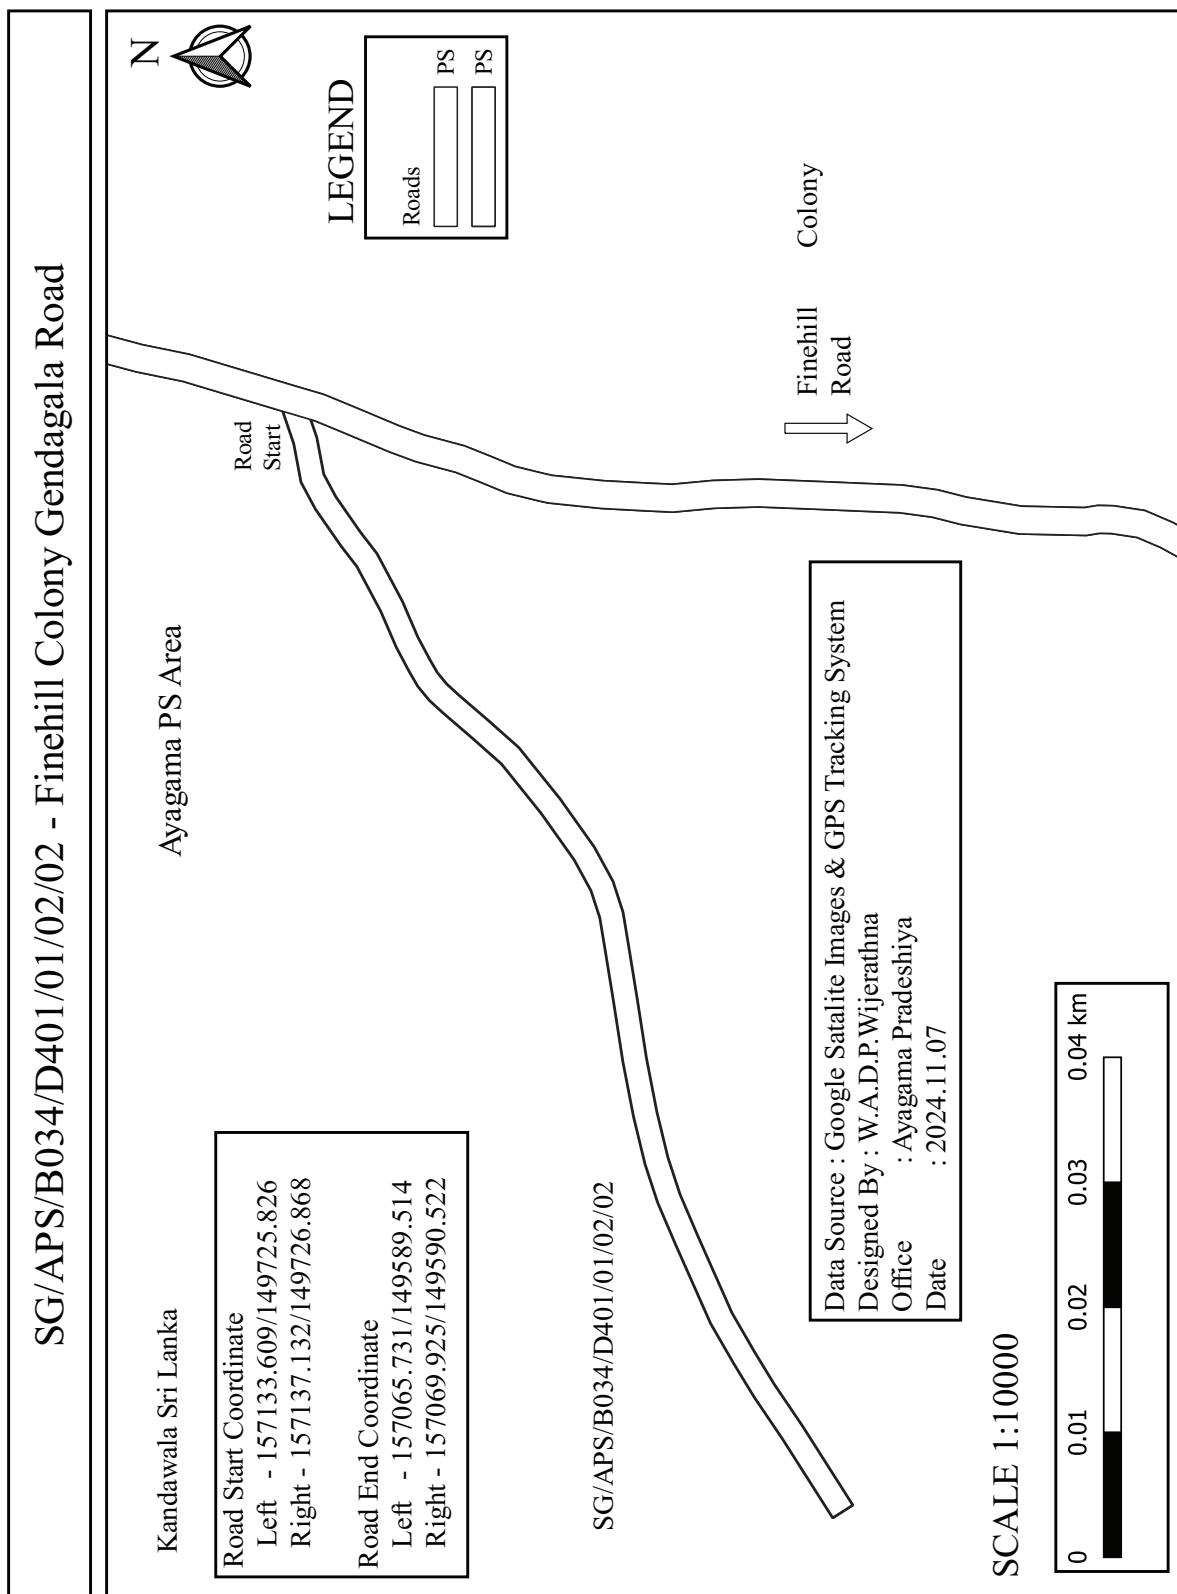





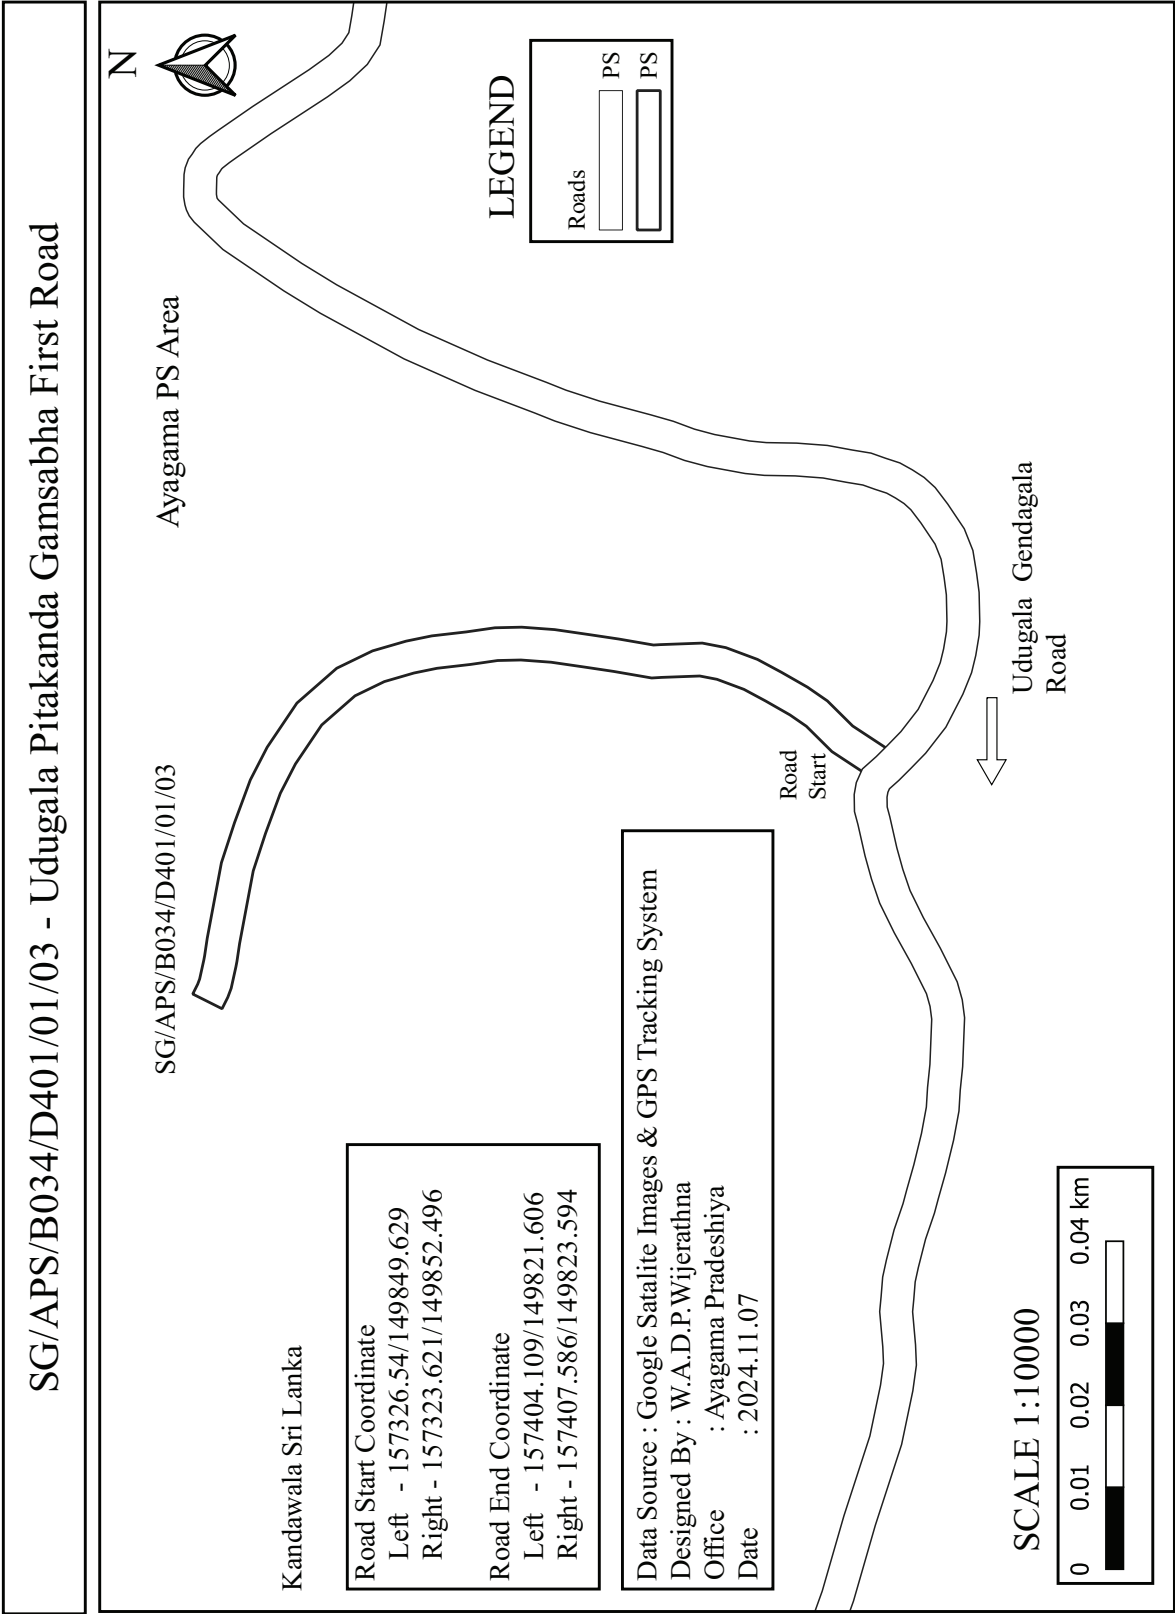


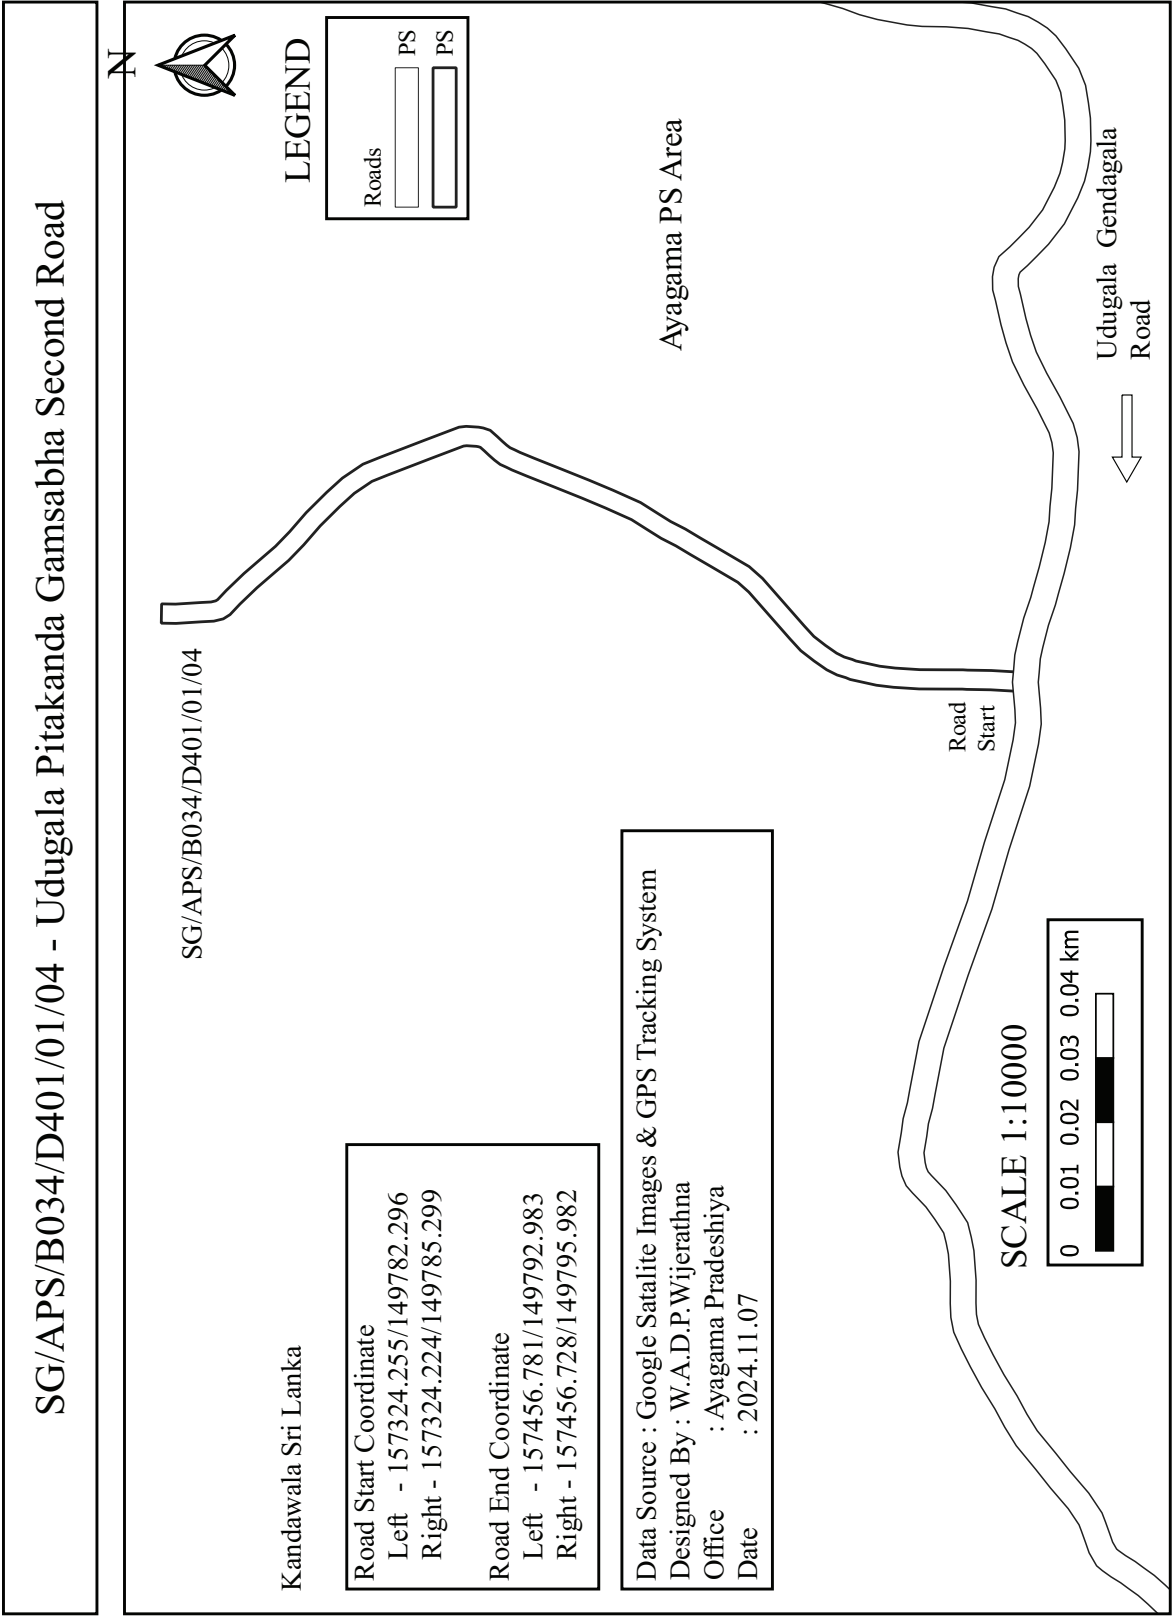





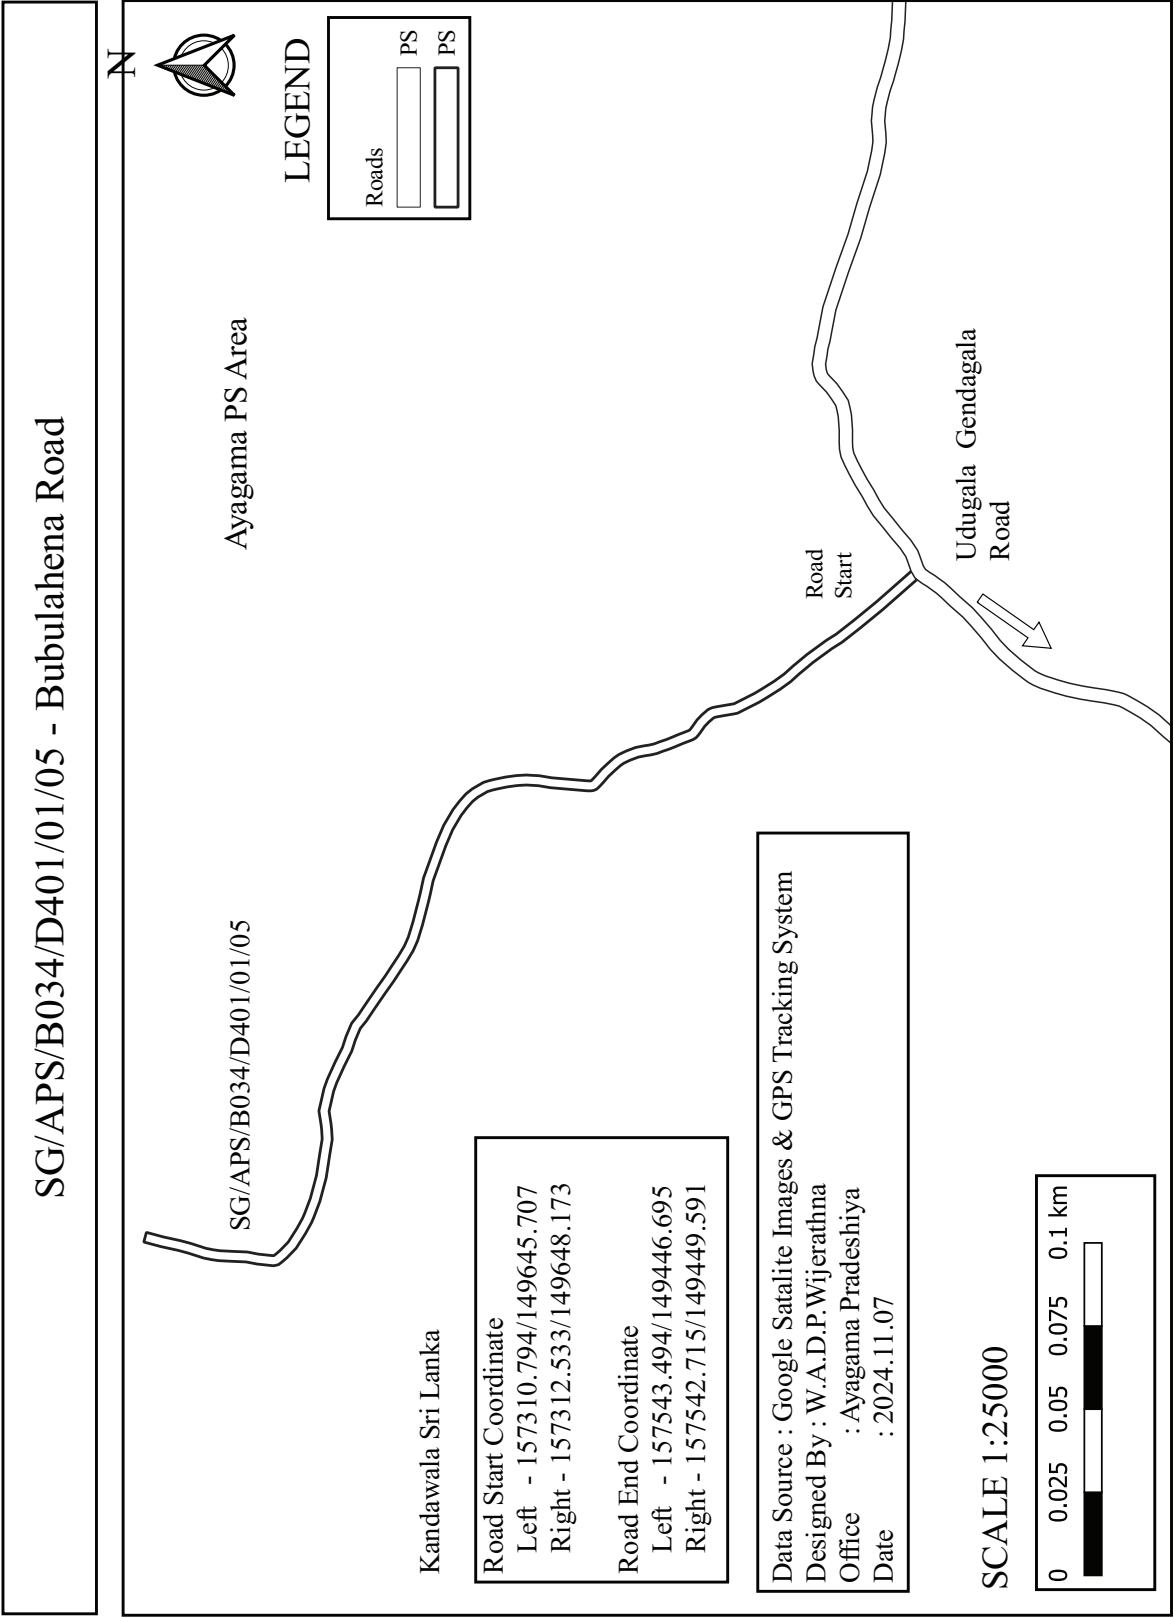


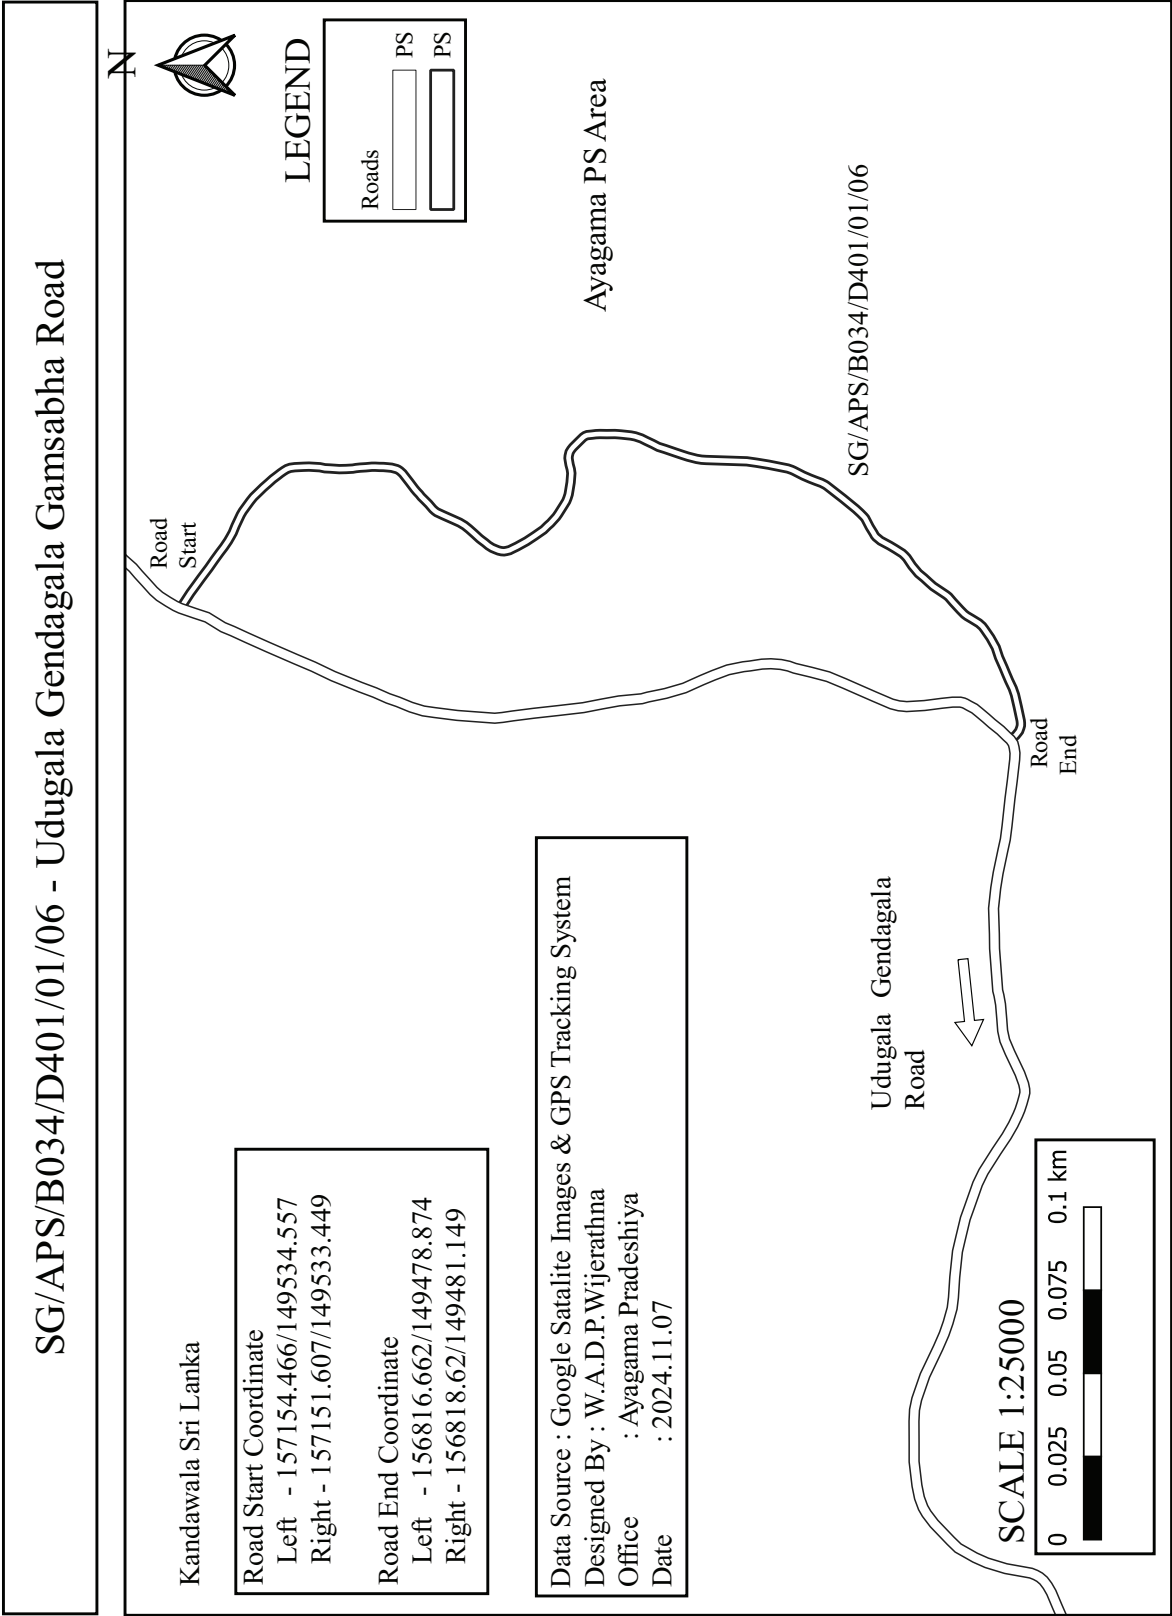


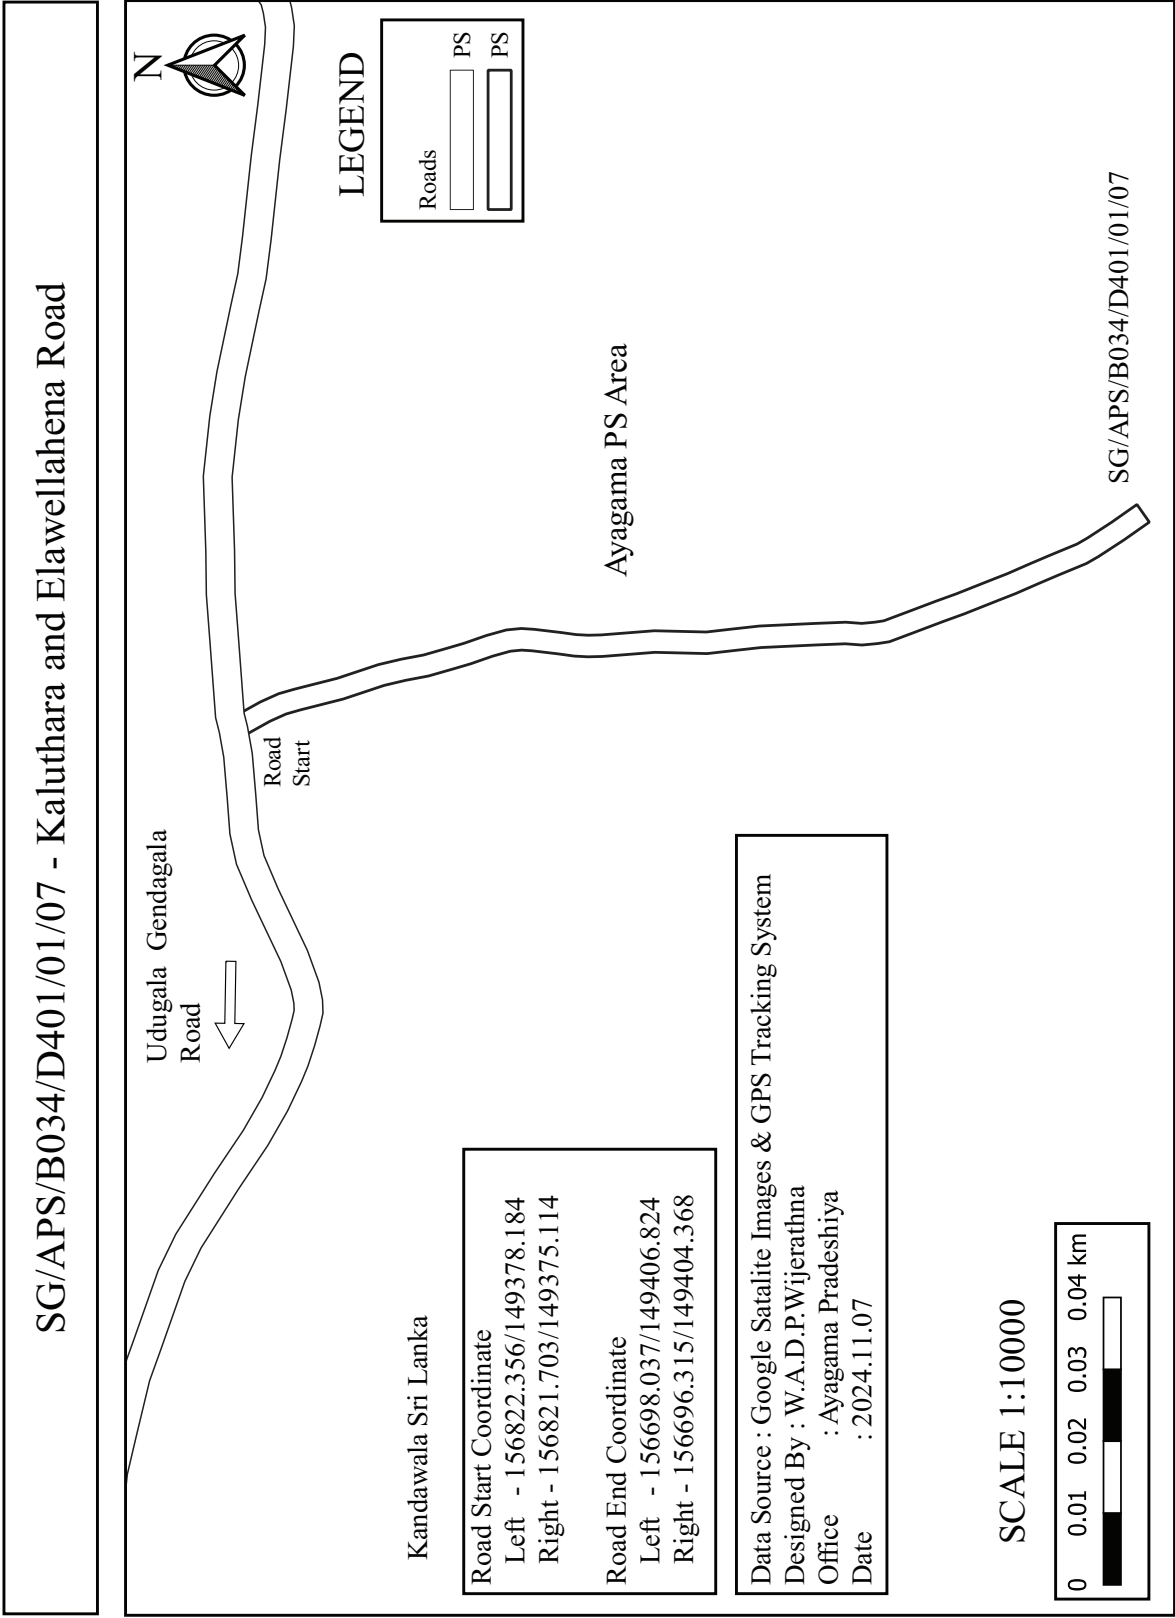


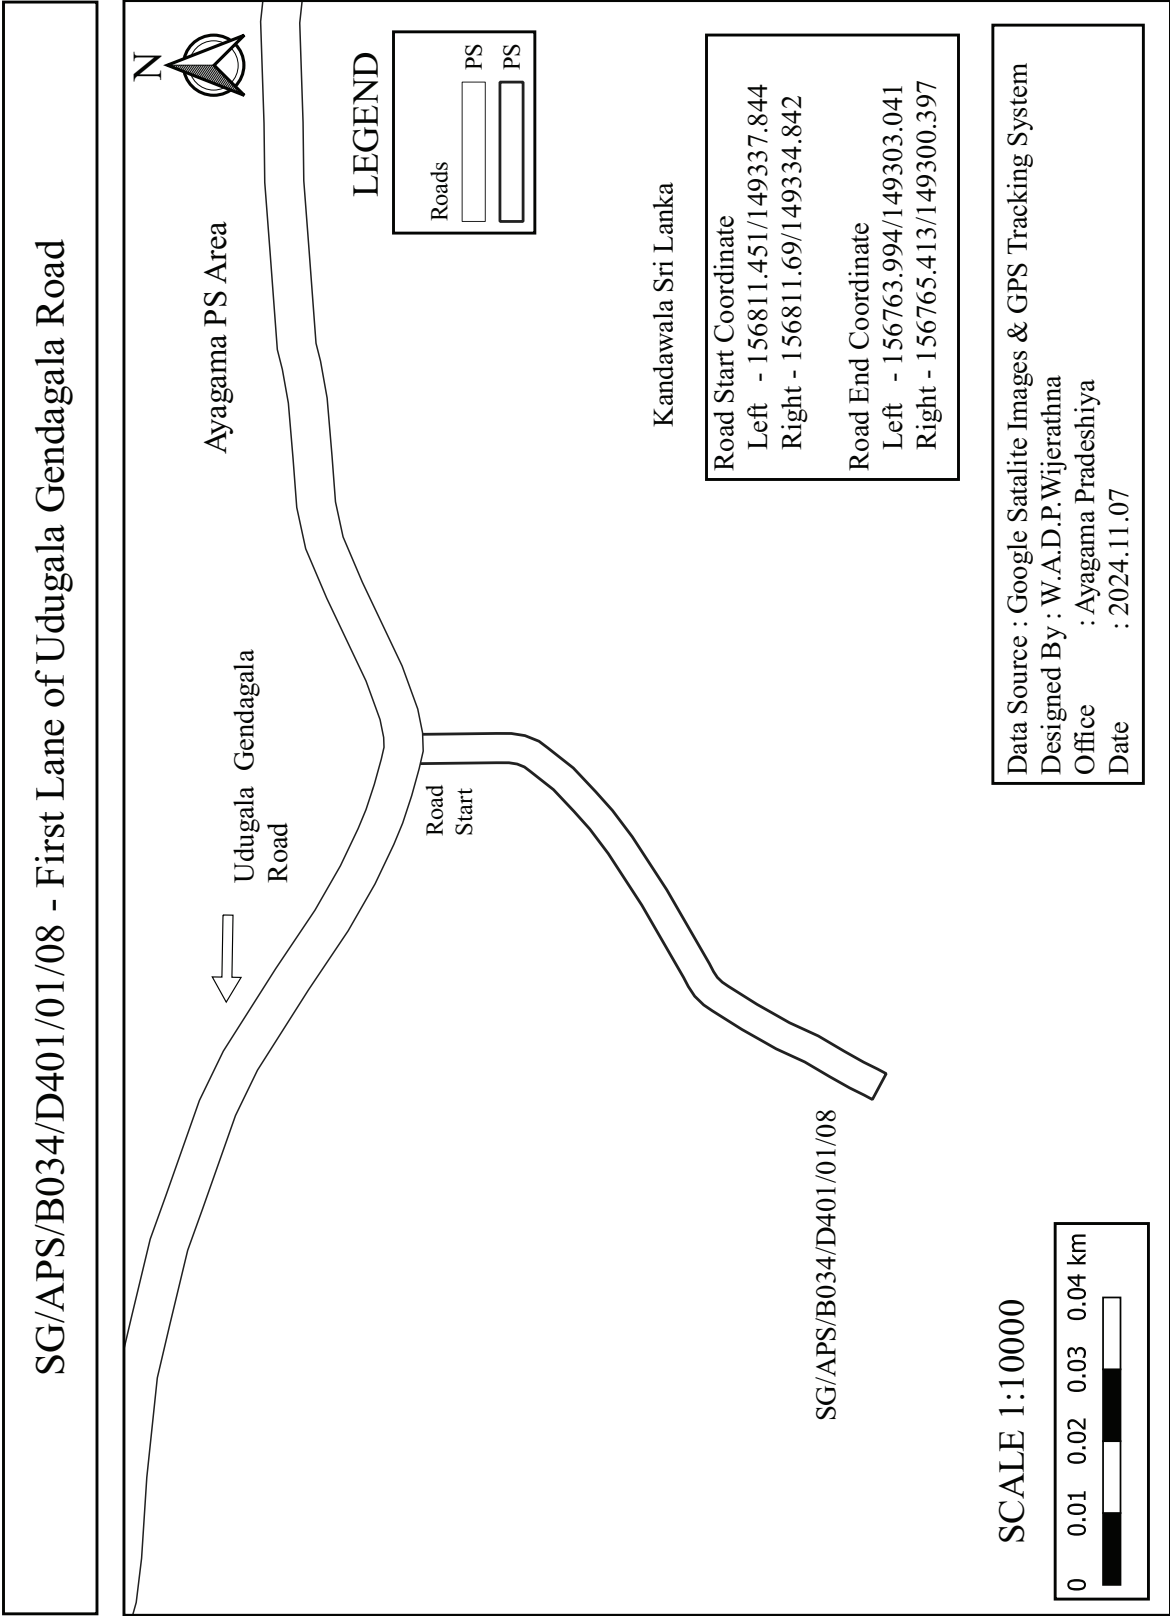

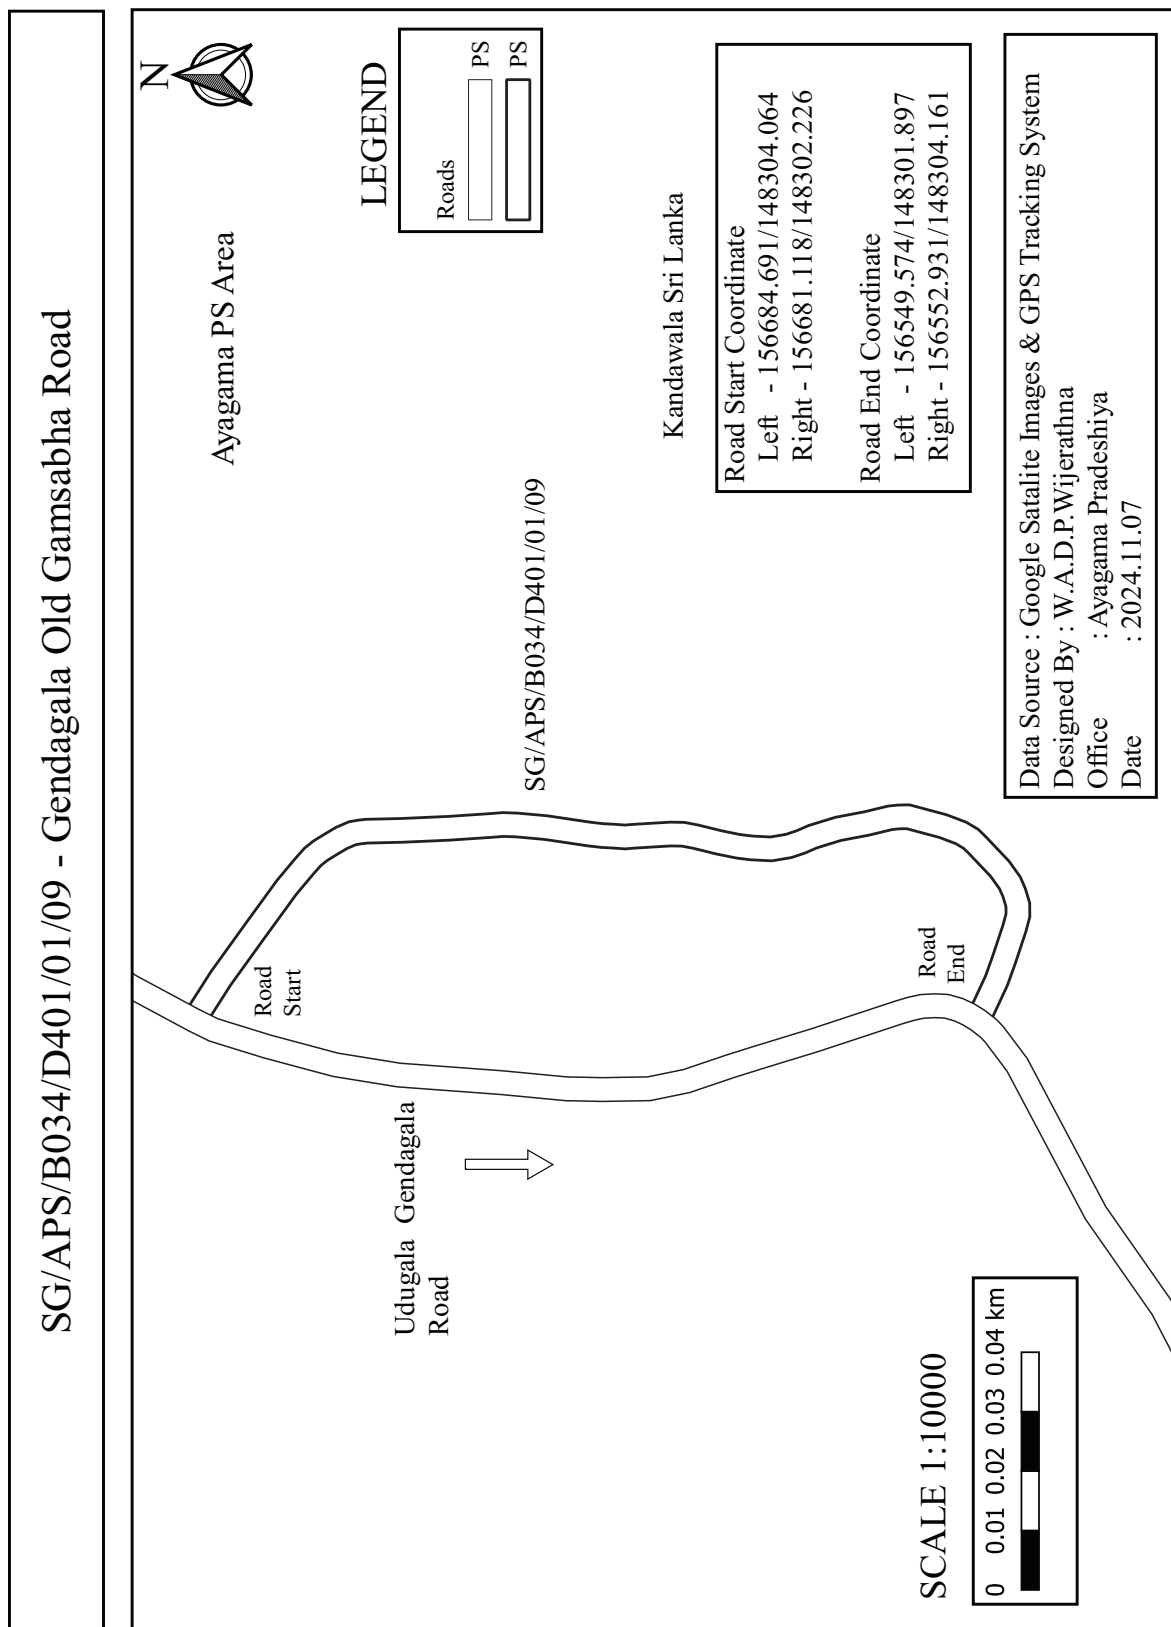


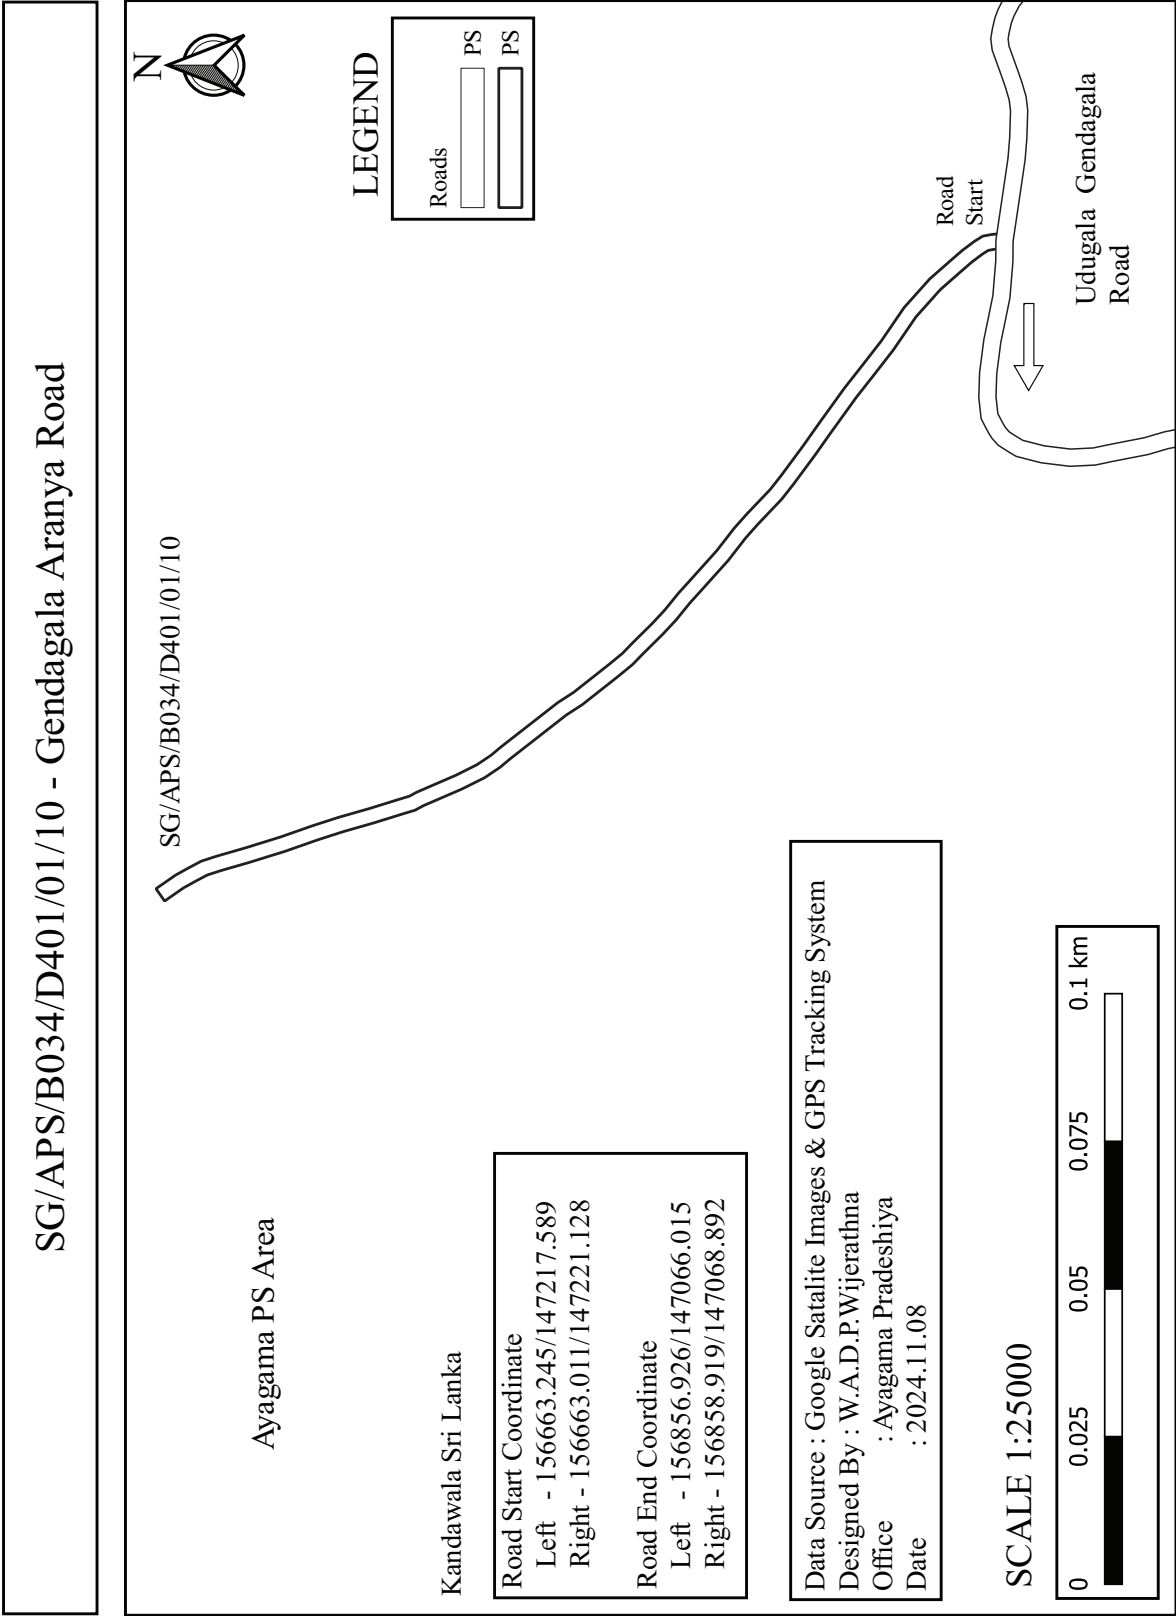


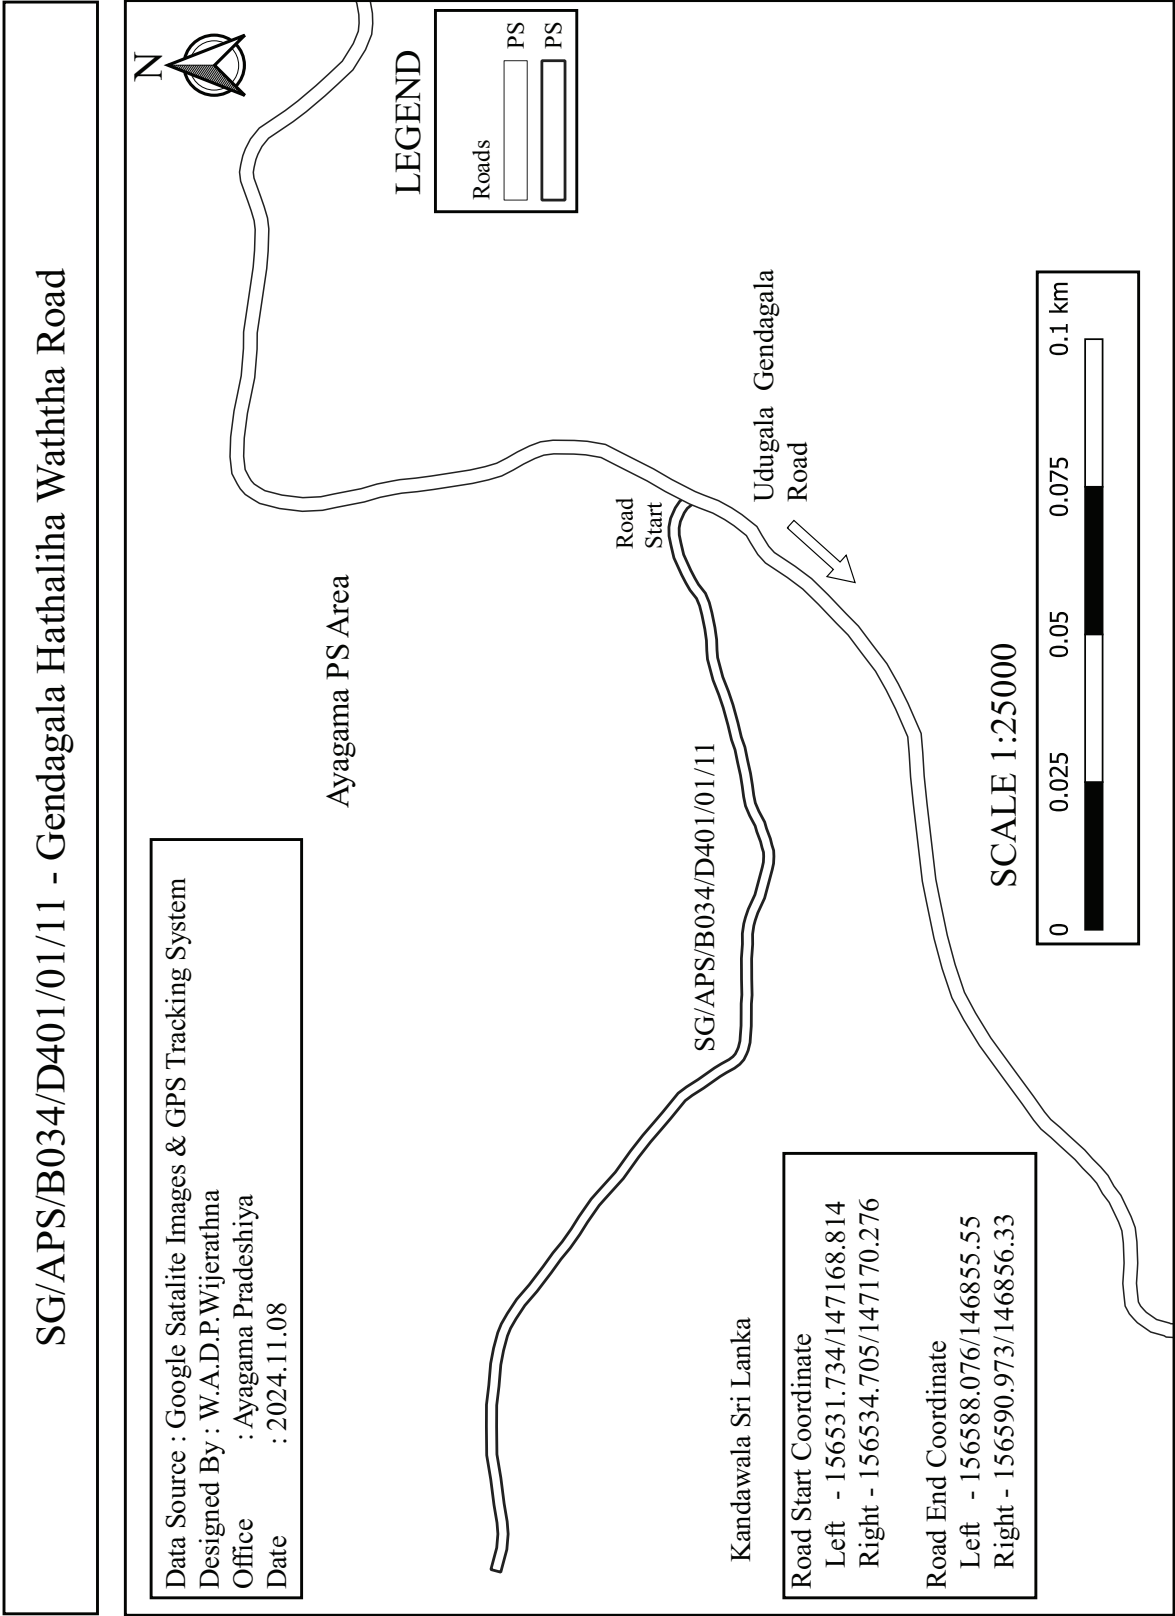


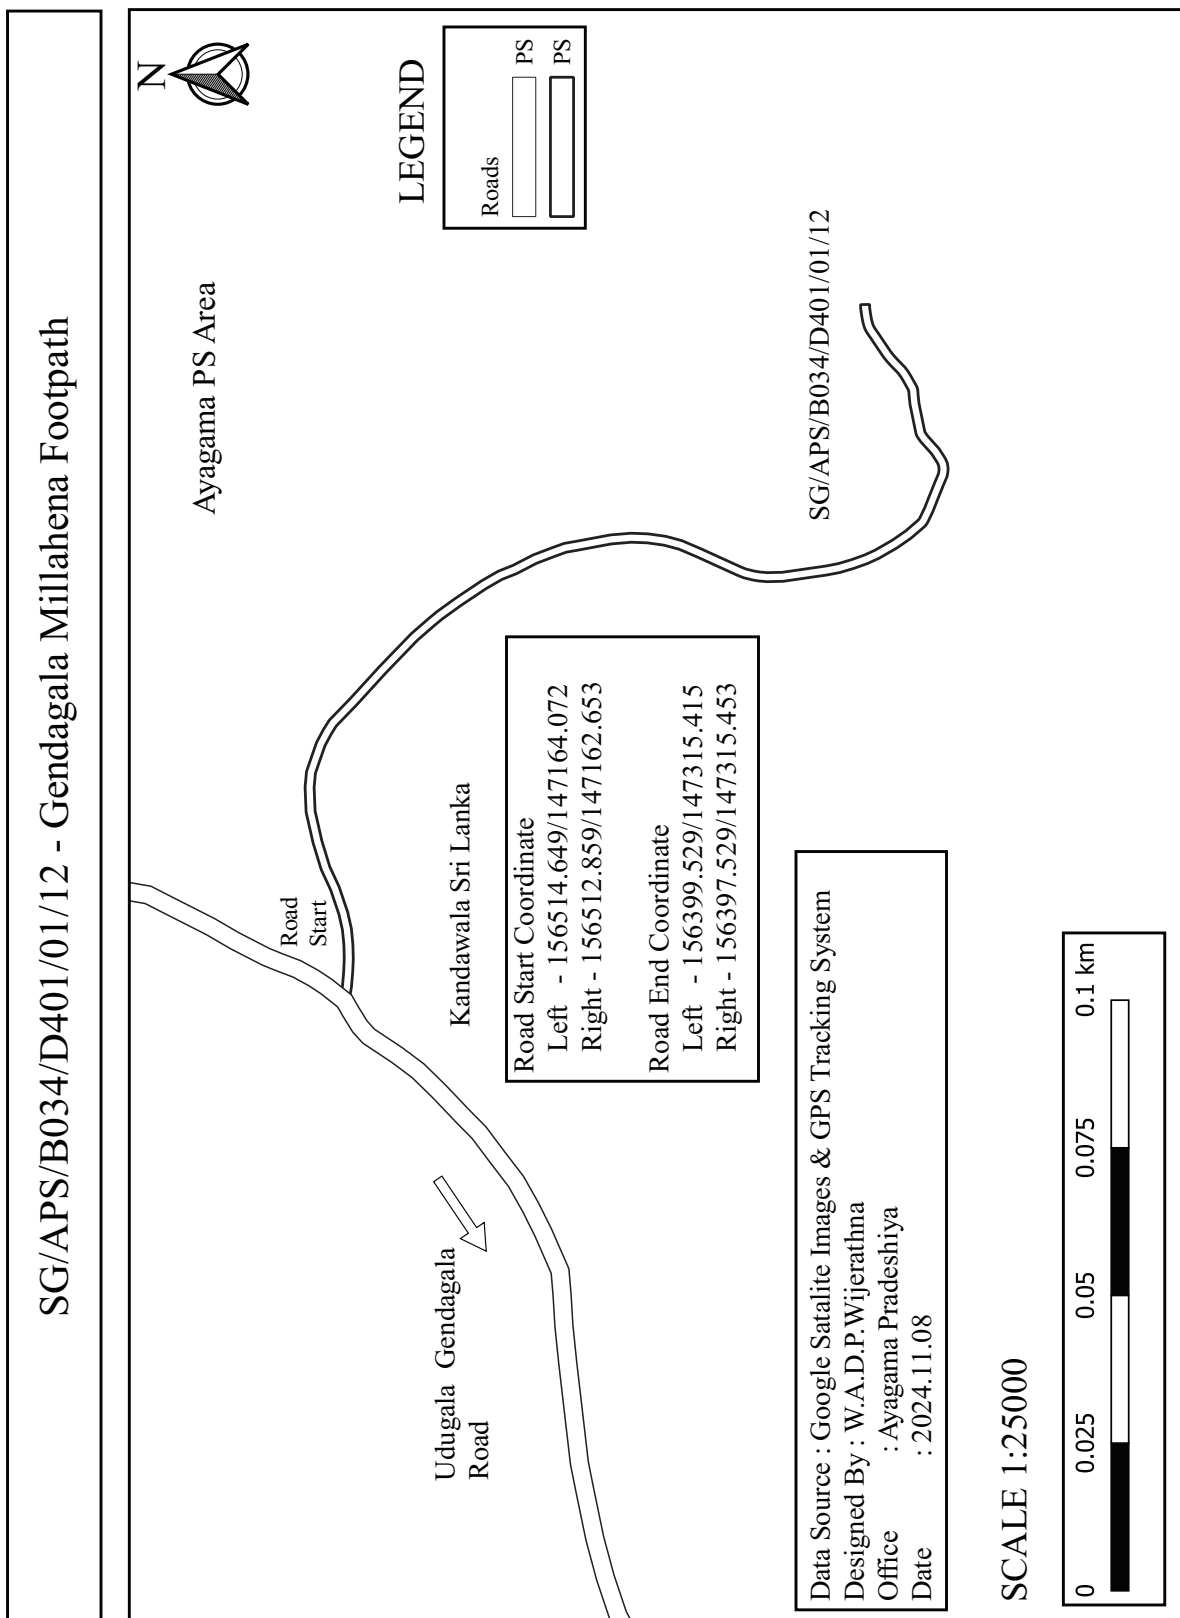





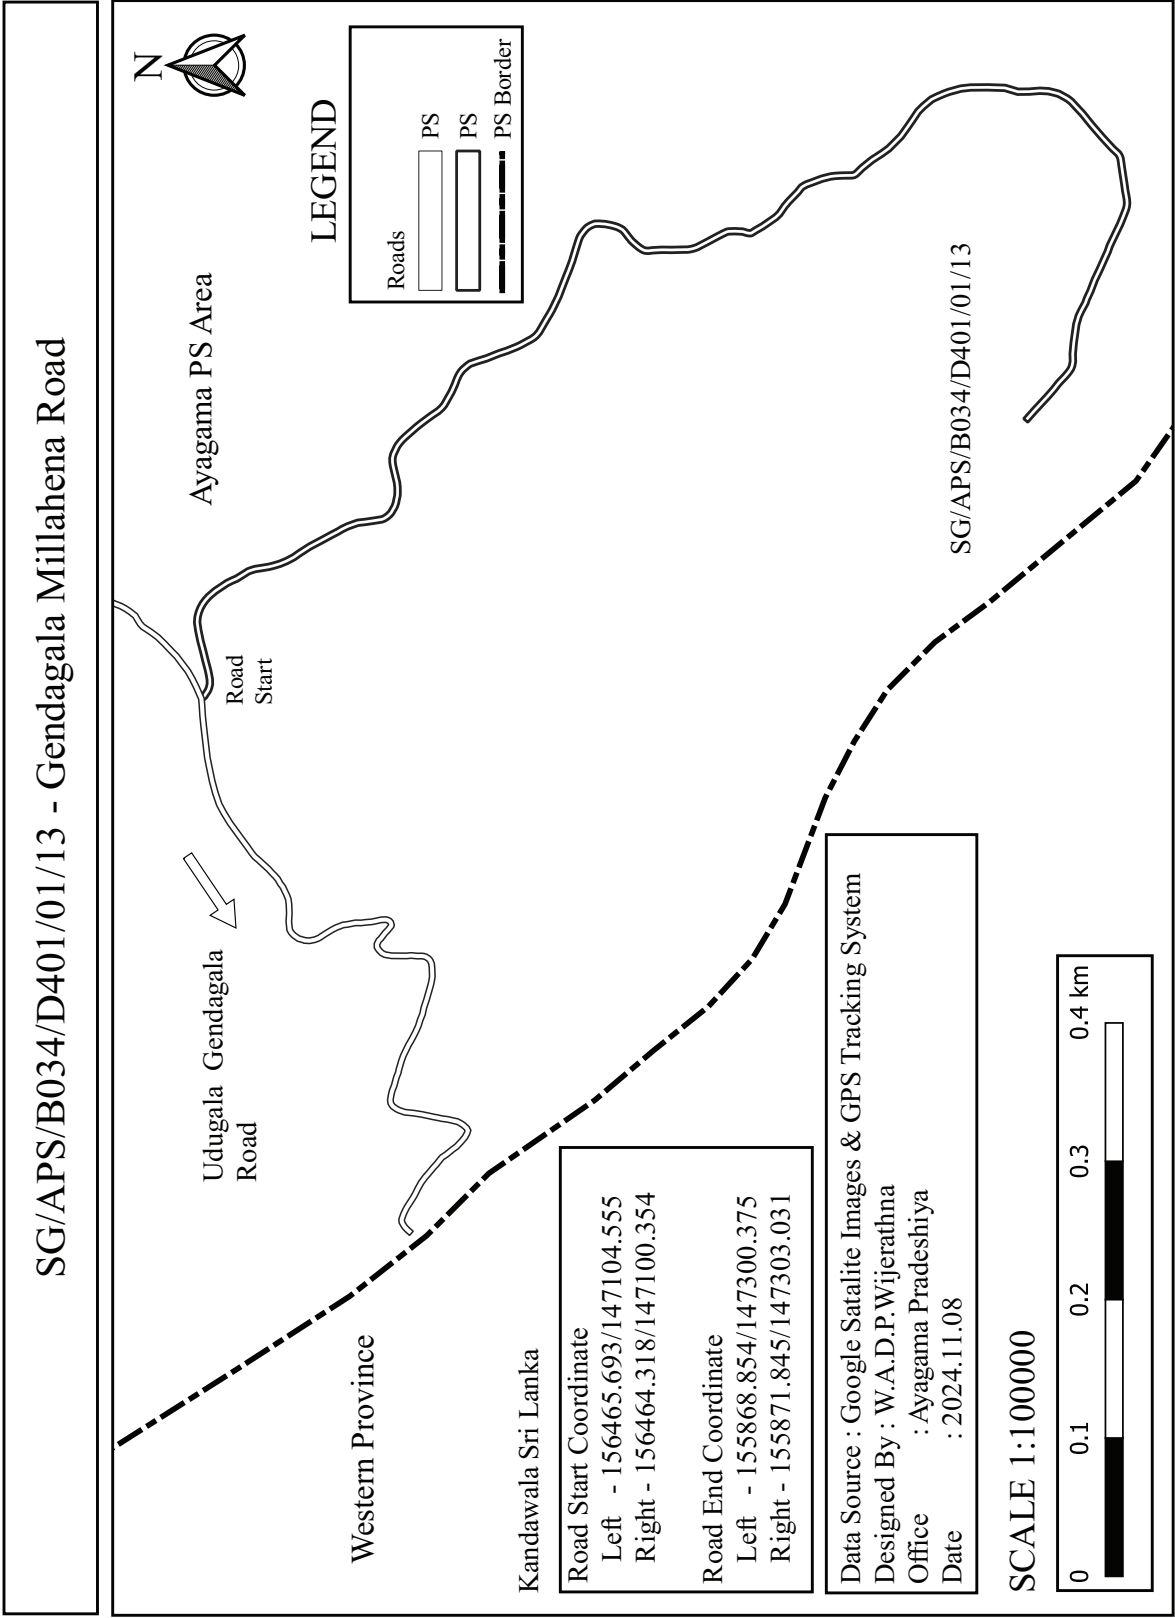


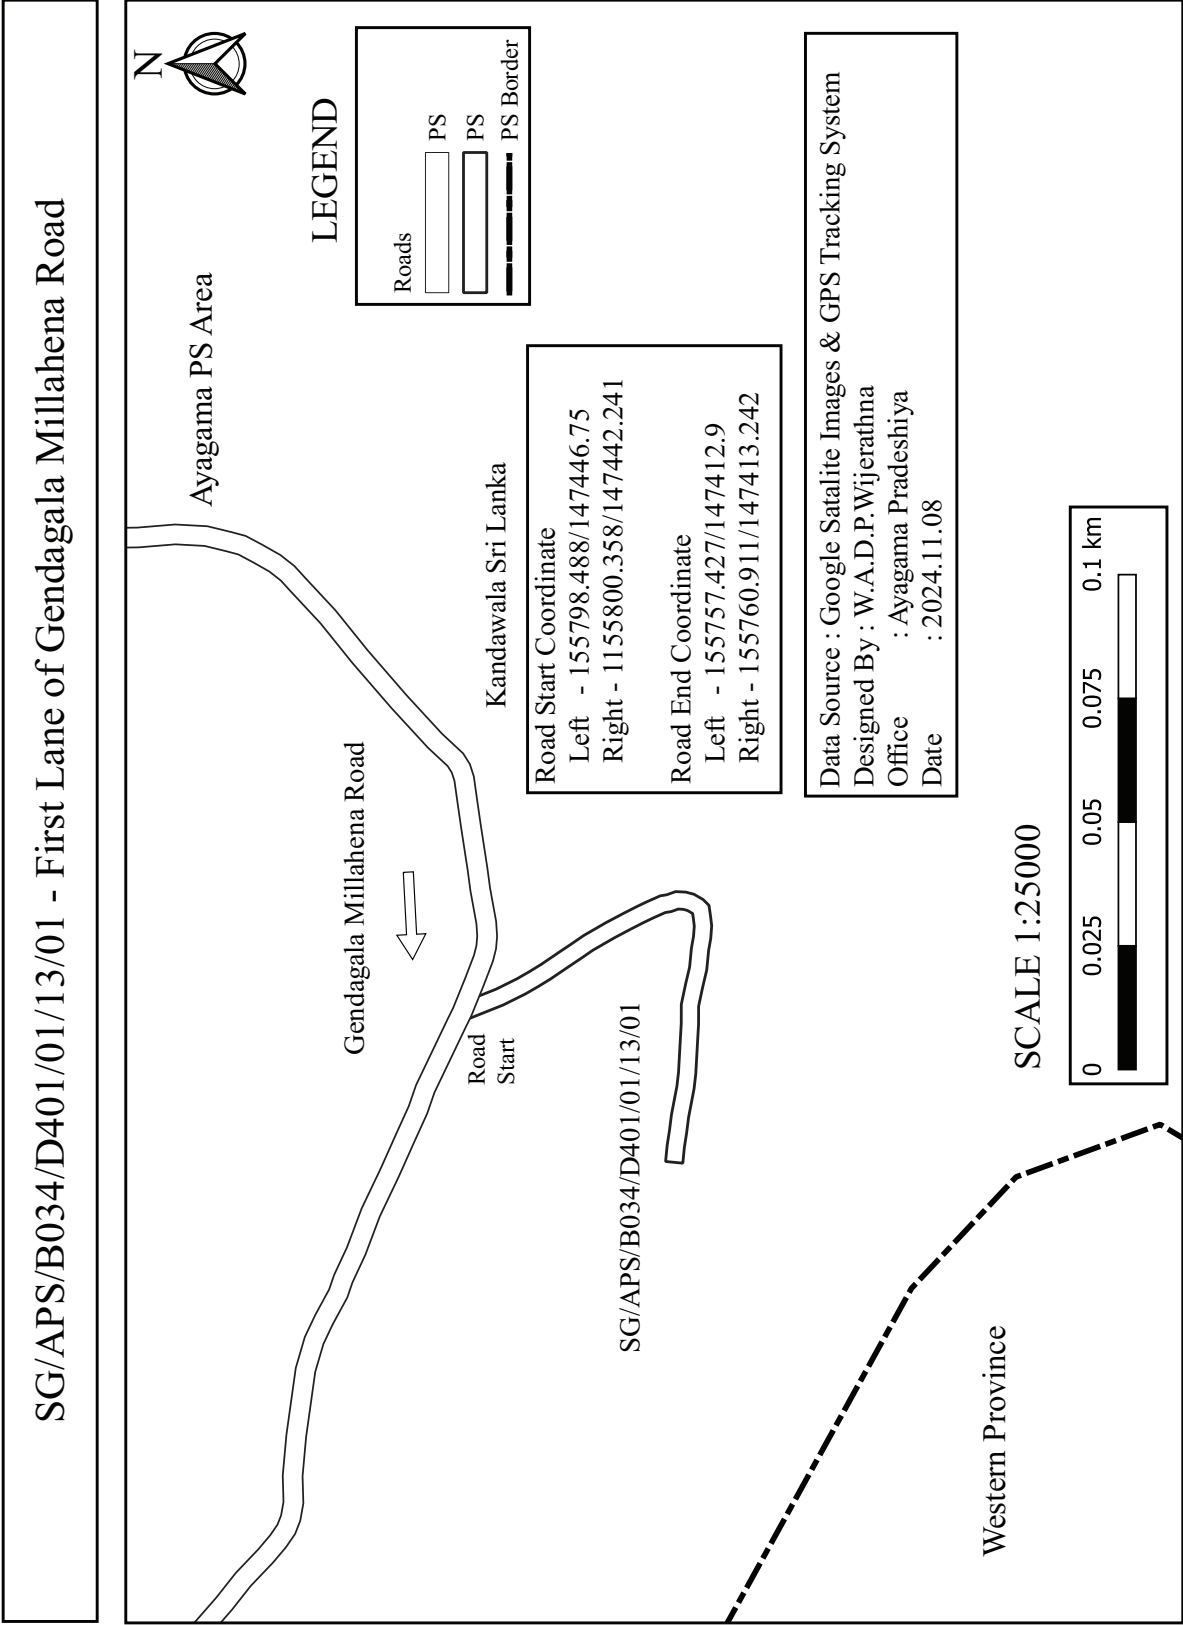


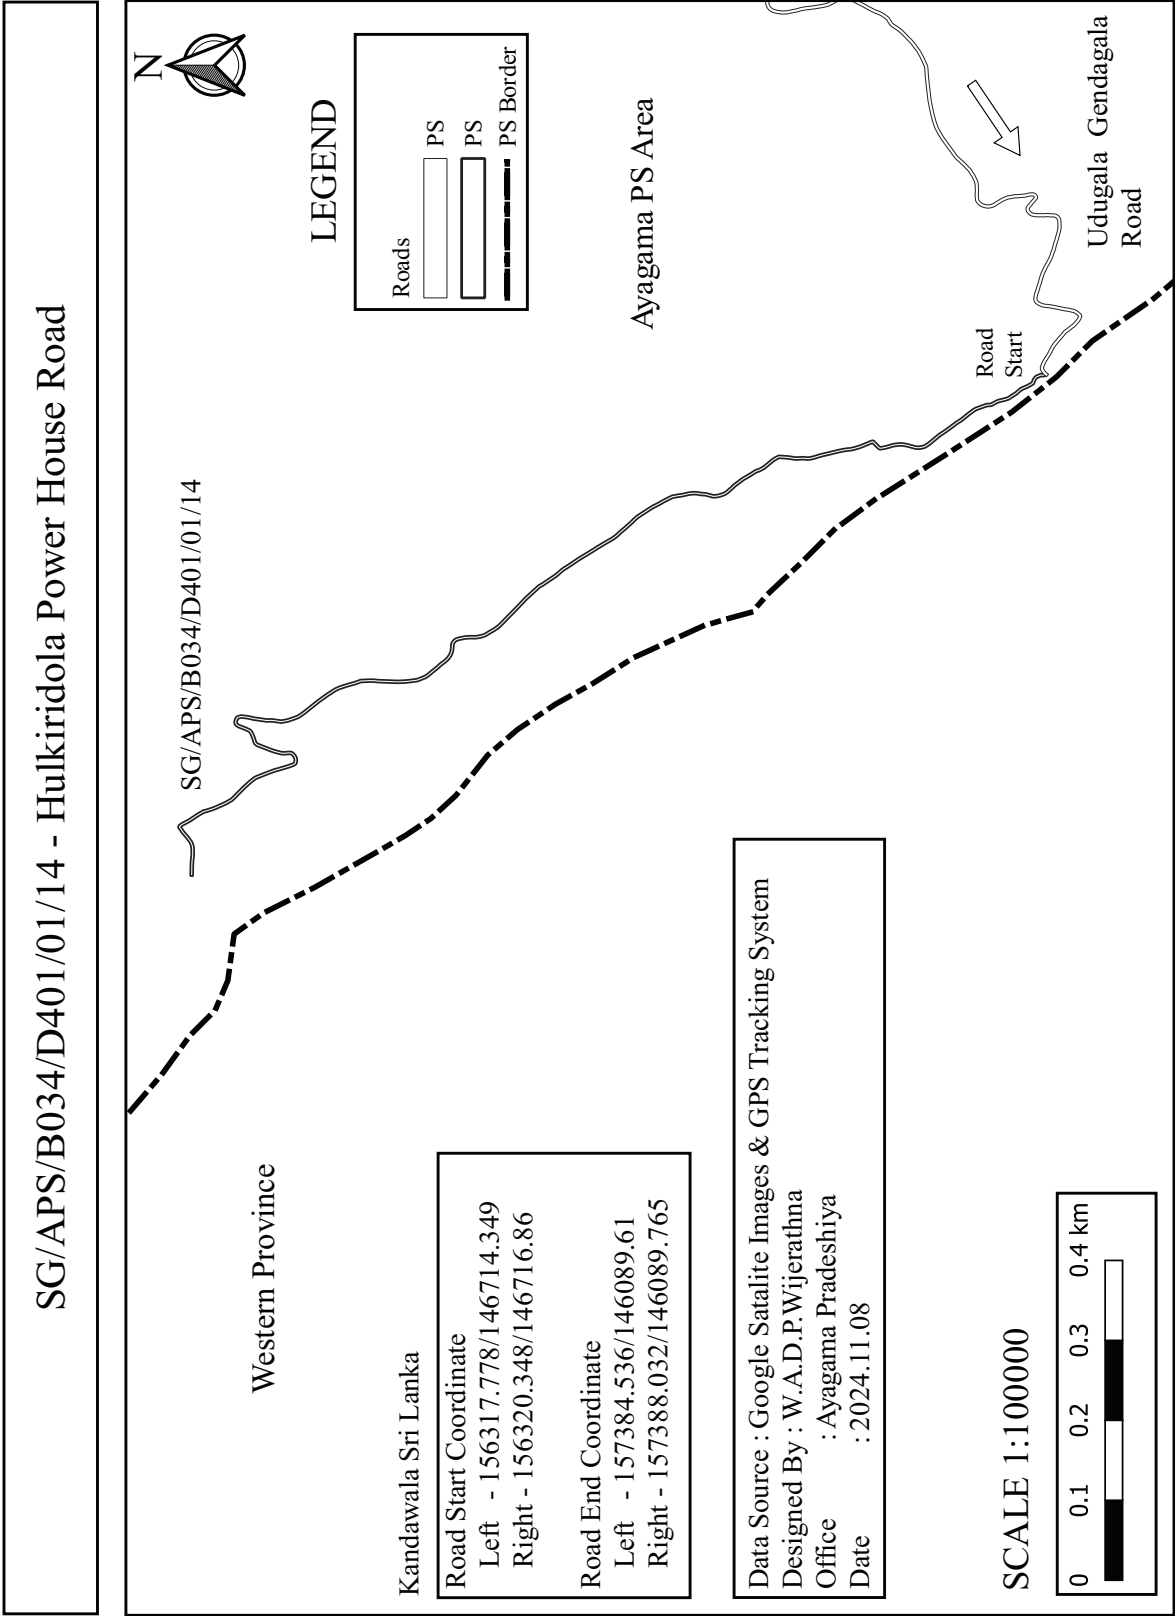


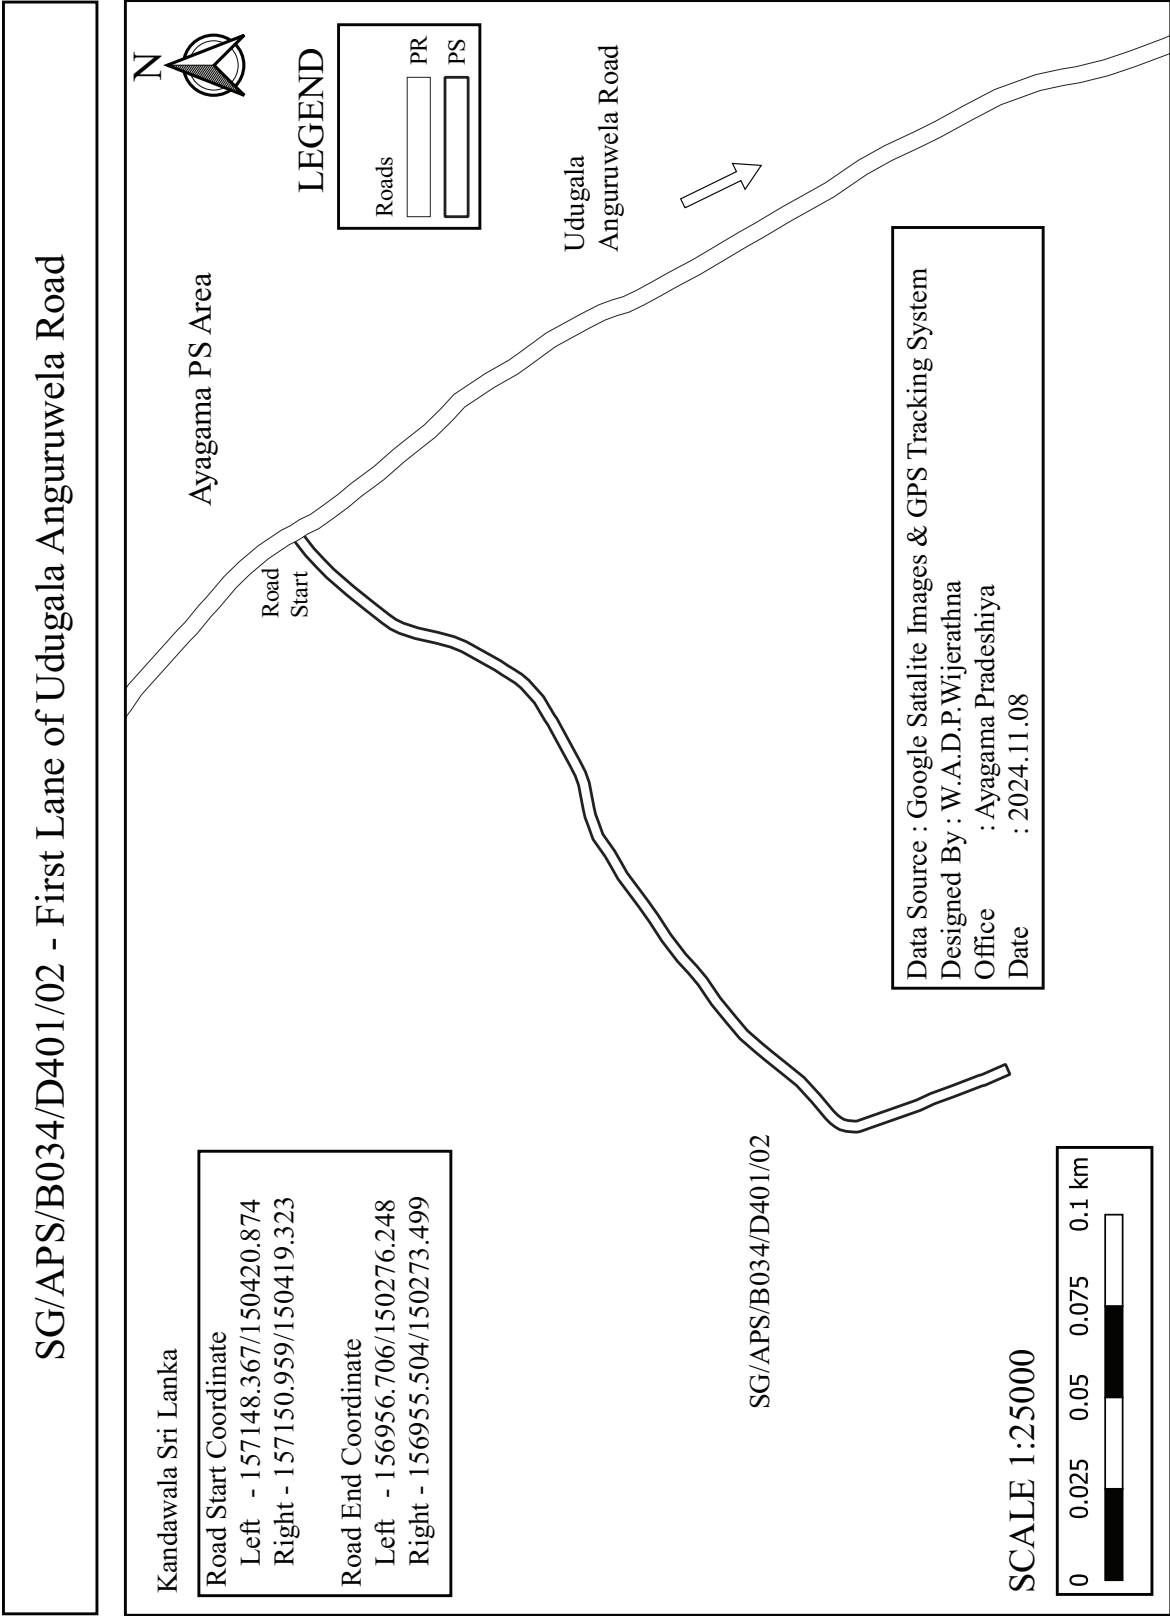

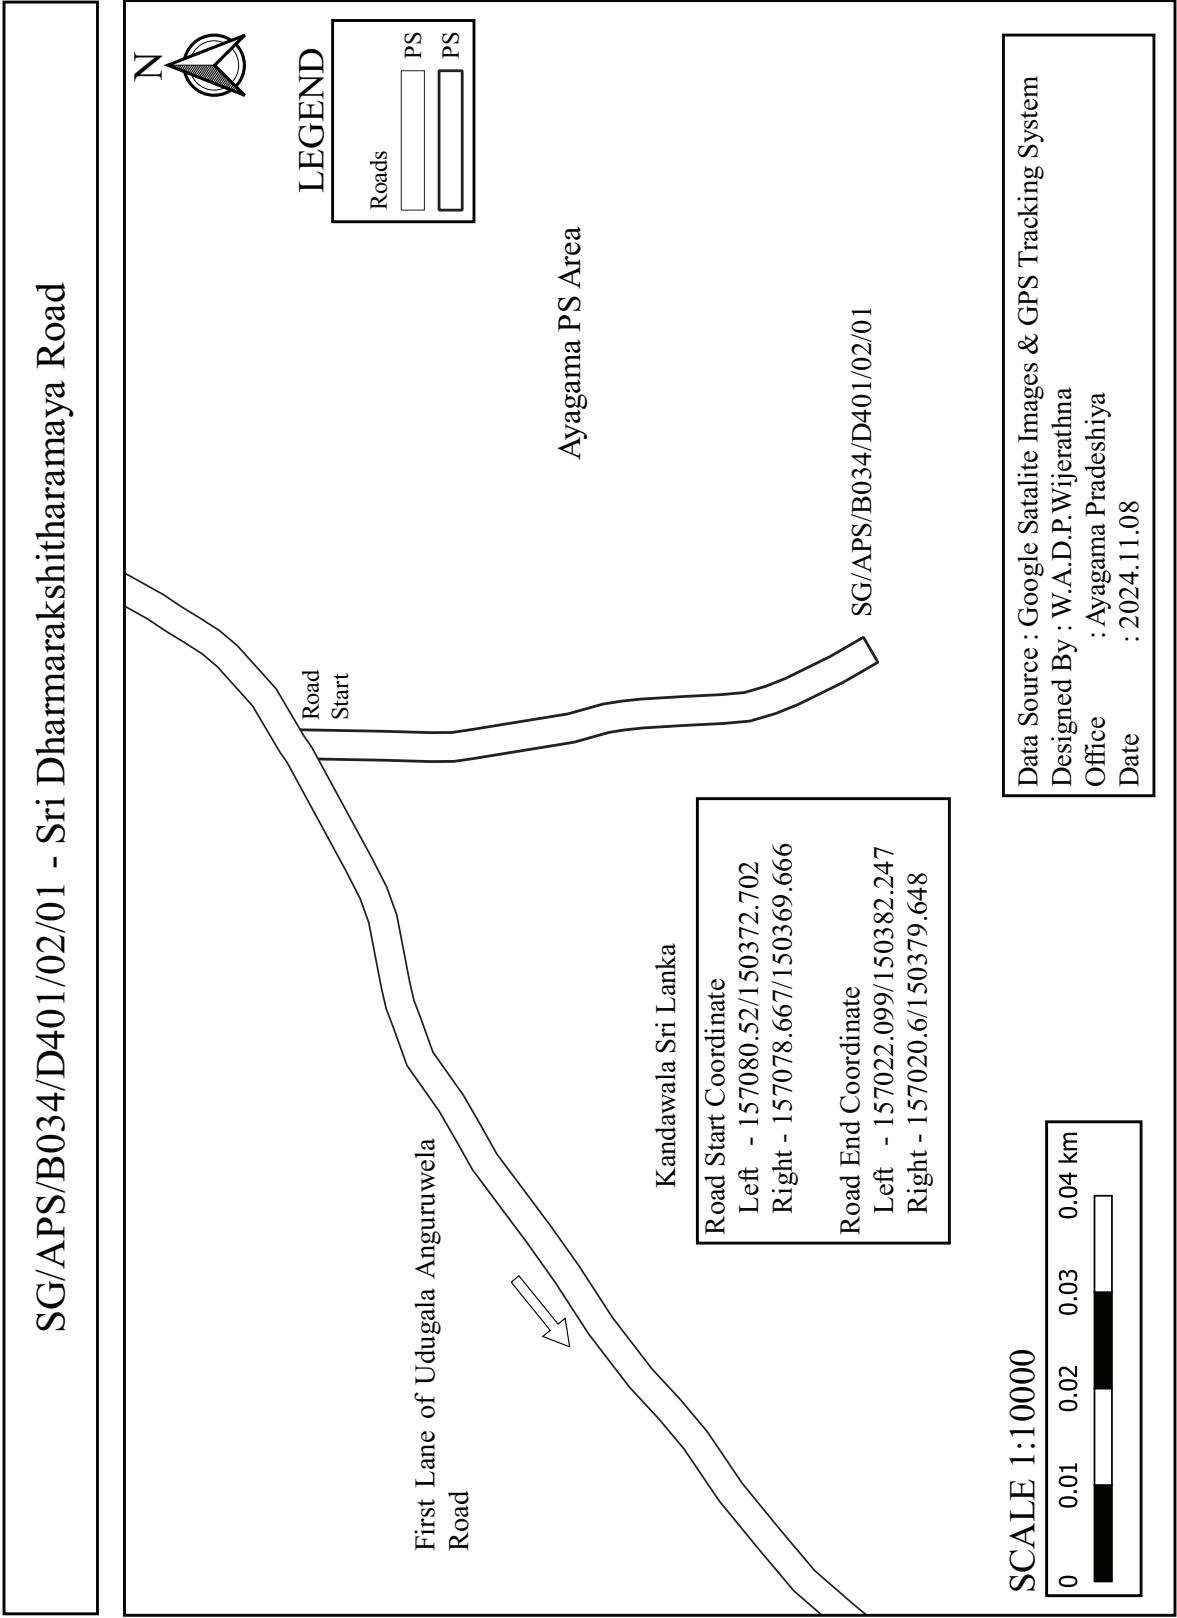

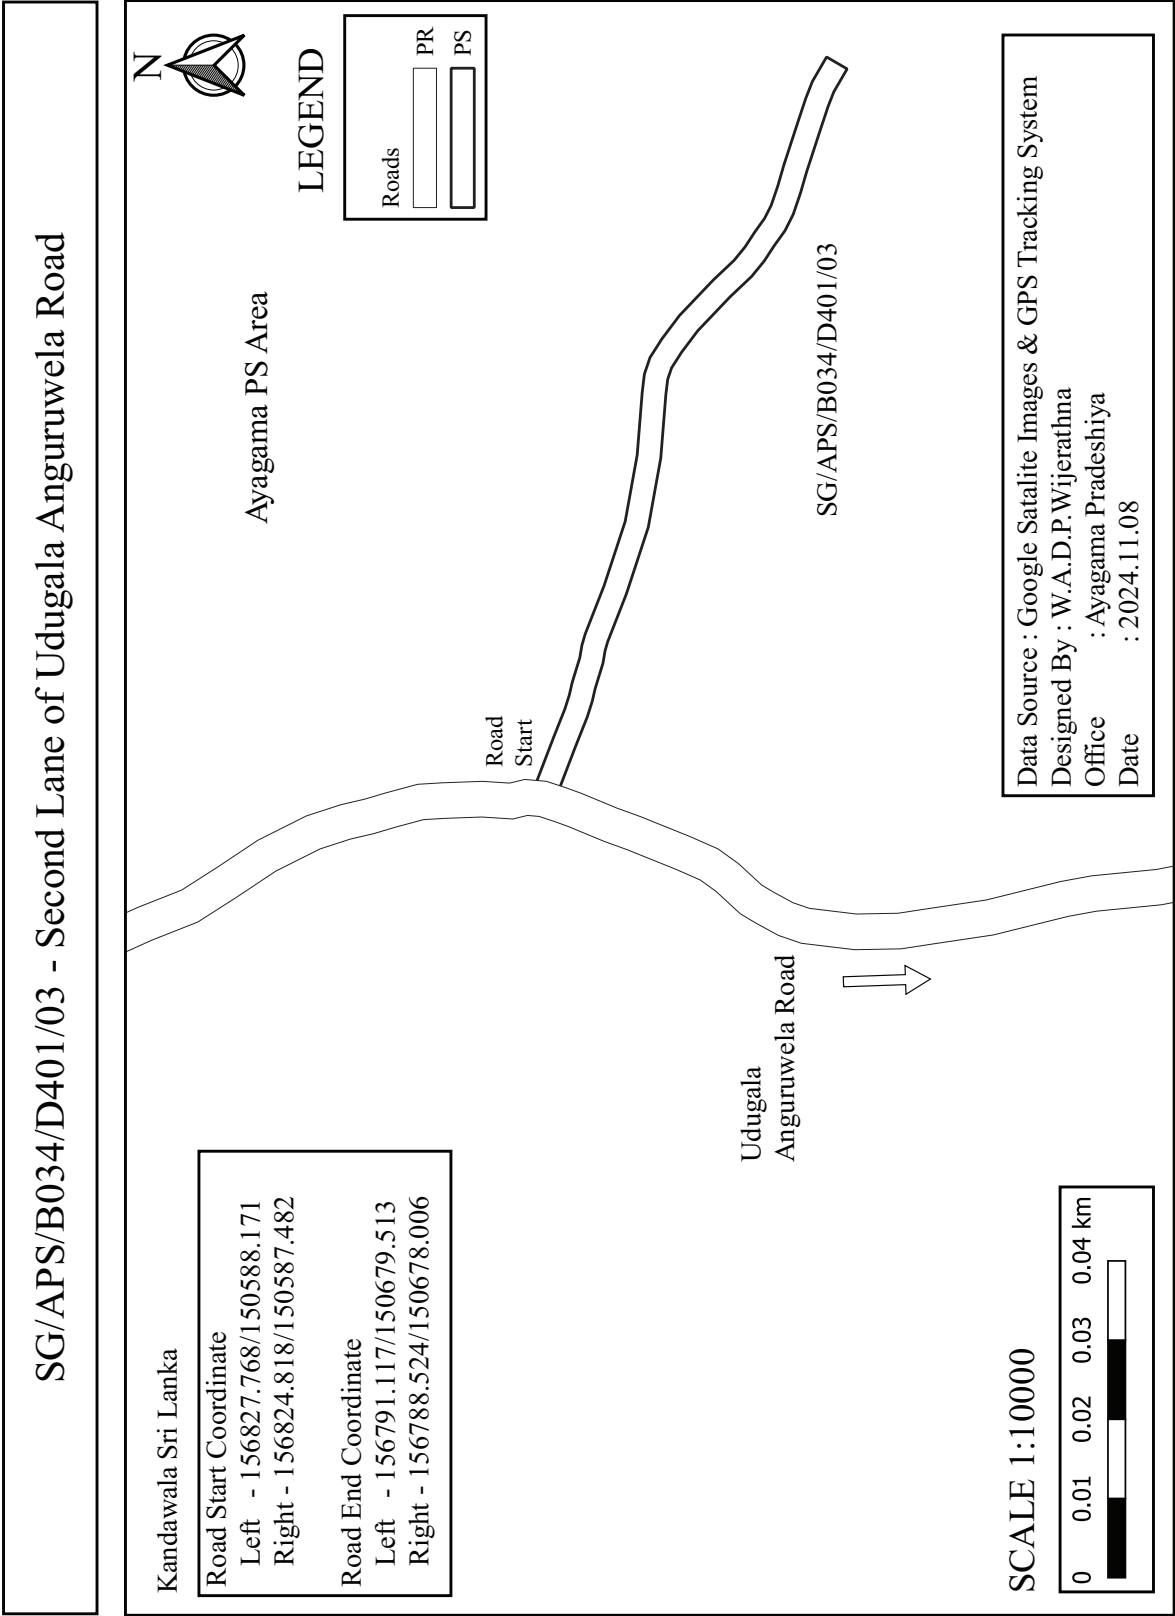

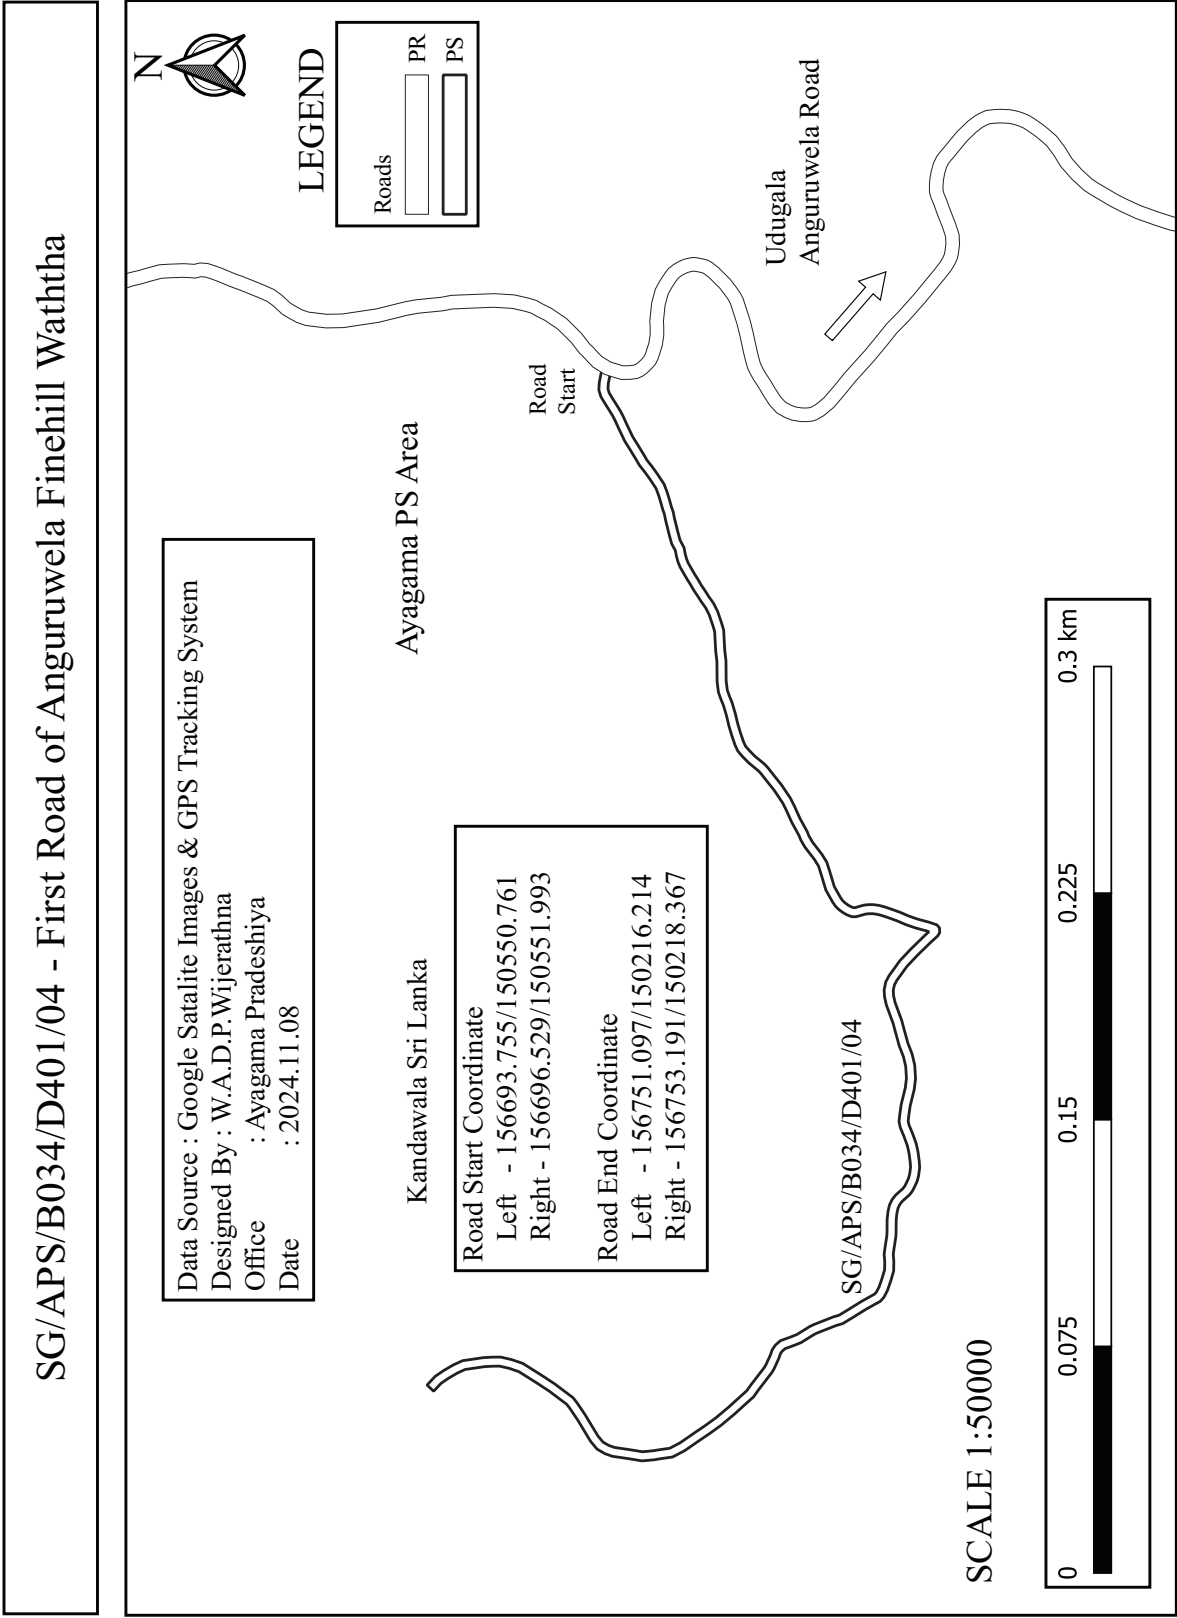

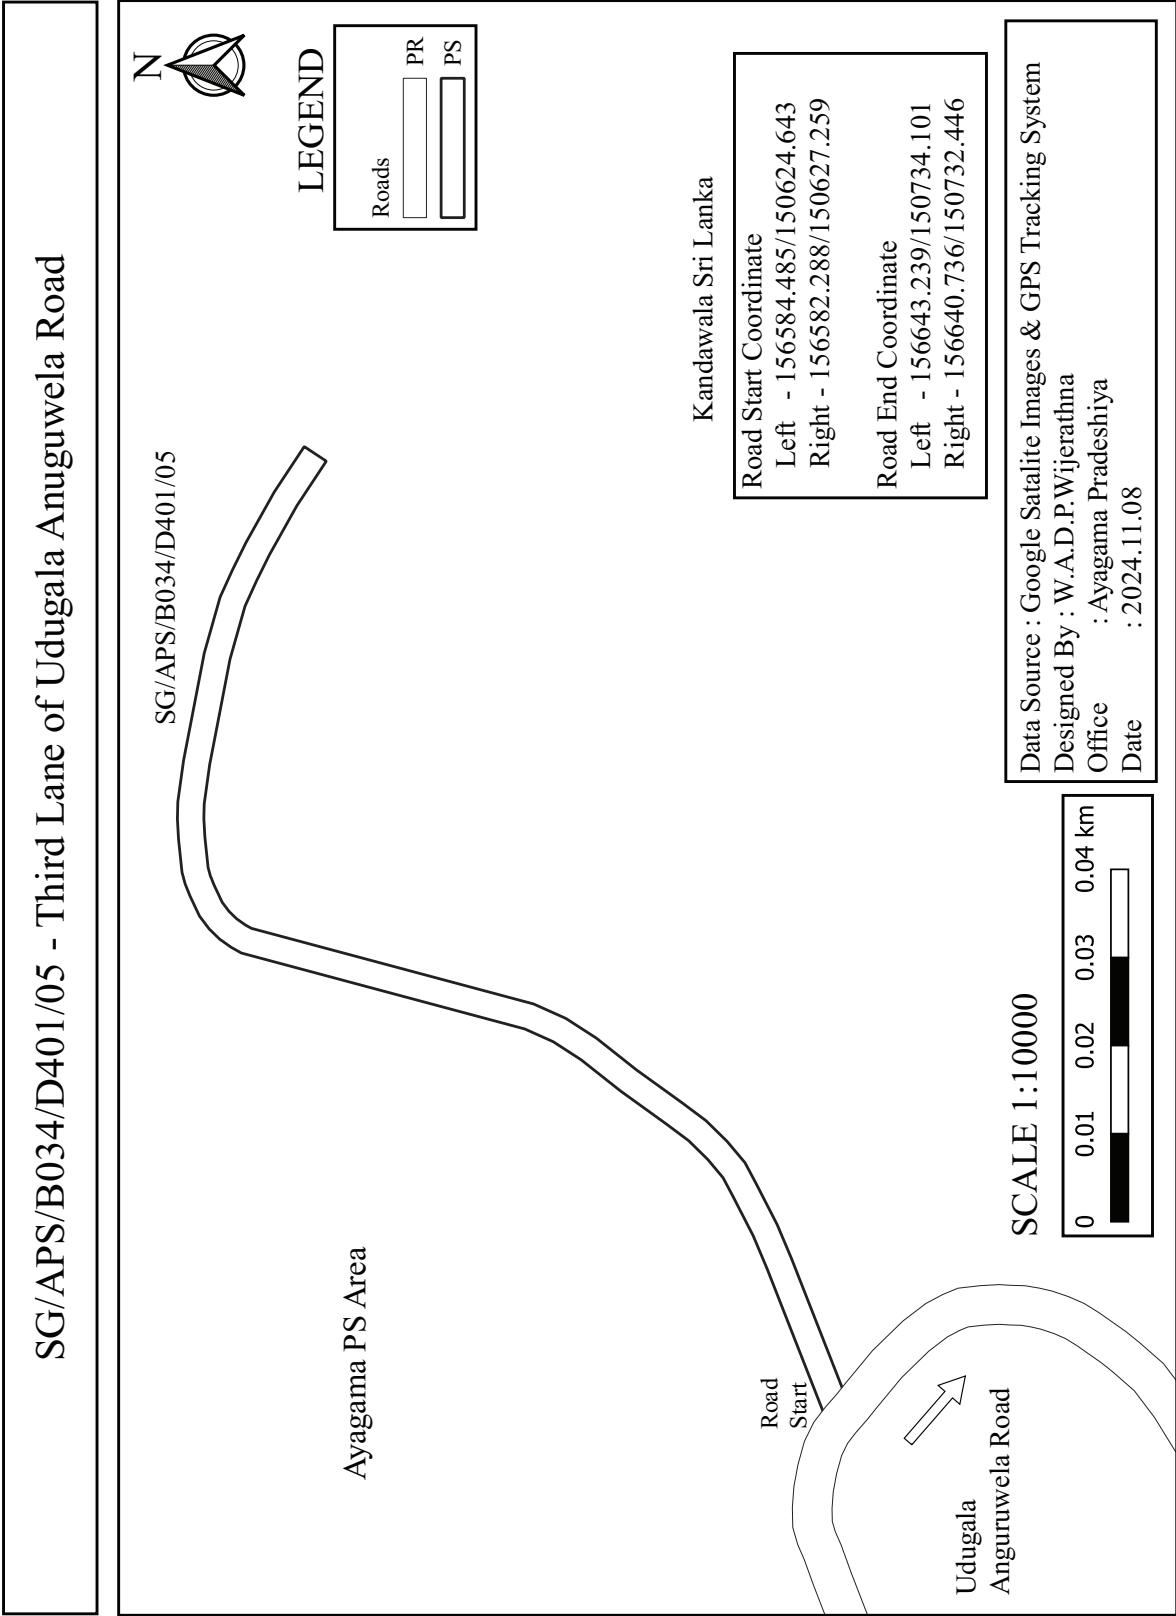

SCALE 1:10000

0

0.01

0.02

0.03

0.04

km

SG/APS/B034/D401/05

Ayagama PS Area

Road Start

Udugala Anguruwela Road



