



ශ්‍රී ලංකා ප්‍රජාතාන්ත්‍රික සමාජවාදී ජනරජයේ ගැසට් පත්‍රය

අති විශේෂ

The Gazette of the Democratic Socialist Republic of Sri Lanka

EXTRAORDINARY

අංක 2429/05 – 2025 මාර්තු මස 24 වැනි සඳුදා – 2025.03.24

No. 2429/05 – MONDAY, MARCH 24, 2025

(Published by Authority)

PART IV (B) – LOCAL GOVERNMENT

Local Government Notifications

Ruwanwella Pradeshiya Sabha

I hereby give notice for information of General Public that as per Secretary's Decision No. 12 and dated 19.12.2024, roads and paths included in this Schedule should be declared as roads and paths belonged to Ruwanwella Pradeshiya Sabha, in terms of task assigned to Pradeshiya Sabhas in Sabaragamuwa Province by the series of orders with regard to publishing notices indicating register and preparation of plans for roads and paths maintained by Sabaragamuwa Province having been declared in Extraordinary Gazette Notification No. 2316/20 dated 24th of January, 2023 by Hon. Governor in Sabaragamuwa Provincial Council read with Section 24 of Pradeshiya Sabha Act, No. 15 of 1987.

If opinion of party claiming to a land that is any road or a path included in the said Schedule is inclusive in any partition of land, I hereby notify that action should be taken to institute an action in the appropriate court before expiration of a period of three months from this Notice for proving own possession for the said land.

Further, I notify that every road and path included in the said Schedule which hasn't been instituted an action before expiration of the said period of three months should be considered as a road or a path belonged to Ruwanwella Pradeshiya Sabha.

P. R. PATHIRANA

Secretary and Executing Officer for
Powers, Duties and Functions
Ruwanwella Pradeshiya Sabhawa.

At Ruwanwella Pradeshiya Sabhawa, Ruwanwella,
17th day of March, 2025.



Third Schedule Eight Section

Serial No.	Code of Road	Name of Road	Starting Coordinates (Kandawala Sri Lanka)		Ending Coordinates (Kandawala Sri Lanka)		Length of Road (Meters)	Normal Width of Road (Meters)	Developed Width (Meters)
			Left	Right	Left	Right			
1	SG/RWP/A21/1	Ritigaha Oya Road	207385.25/ 145085.475	207388.165/ 145083.295	207312.796/ 145057.926	207313.317/ 145054.324	93.8	3.65	2.74
2	SG/RWP/A21/2	Wekada 1st Lane	207586.053/ 144923.7	207588.372/ 144921.698	207506.548/ 144939.056	207506.235/ 144936.032	94.41	3.04	2.43
3	SG/RWP/A21/3	Gonaramba - Ihlagagama Road	207659.873/ 144883.025	207656.338/ 144885.907	208196.163/ 145331.986	208191.683/ 145332.876	799.61	4.57	3.04
4	SG/RWP/A21/4	Gonaramba Badagatawala Road	207670.238/ 144854.635	207673.51/ 144851.766	207671.924/ 144855.933	207225.542/ 144694.799	821.19	4.26	2.74
5	SG/RWP/A21/4/1	Bandarahena Road	207462.497/ 144727.763	207459.367/ 144722.958	207329.085/ 144732.663	207328.043/ 144728.532	136.44	4.26	2.74
6	SG/RWP/A21/4/2	Badagatawala Colony Pahala Road	207458.408/ 144714.35	207466.235/ 144725.226	207193.492/ 144471.326	207193.26/ 144466.471	584.86	4.87	2.74
7	SG/RWP/A21/5	Gonaramba Kande Wihara Road	207812.256/ 144755.621	207809.795/ 144757.678	207899.707/ 144961.361	207896.774/ 144960.56	264.99	3.04	2.43
8	SG/RWP/A21/6/1	Warawala Doranuwa Road	207750.329/ 144134.186	207750.839/ 144129.236	206899.945/ 144138.253	206899.917/ 144133.377	984.81	4.87	3.04
9	SG/RWP/A21/6/1/1	Sama Mawatha	207364.466/ 144195.157	207368.664/ 144192.59	207370.504/ 144014.635	207373.449/ 144015.391	266.24	3.04	2.43
10	SG/RWP/A21/6/1/2	Warawala Doranuwa Road 1st Lane	207104.105/ 144247.424	207107.901/ 144249.357	207124.666/ 143956.033	207129.088/ 143952.471	316.19	4.26	3.04
11	SG/RWP/A21/6/1/2/1	Walawwaththa Dewata Road	207146.736/ 144202.358	207144.824/ 144206.281	207261.272/ 143914.435	207261.578/ 143918.684	396.39	4.26	3.04
12	SG/RWP/A21/7	Pol Aththa Wela Road	207745.3/ 144037.931	207748.639/ 144041.645	208003.638/ 144063.391	208008.497/ 144063.258	294.9	4.87	3.04
13	SG/RWP/A21/8	Mudugamuwa 1st Lane Part 01	207670.31/ 143977.107	207667.791/ 143974.449	207602.375/ 144084.975	207599.03/ 144083.537	136.37	3.65	3.04

Serial No.	Code of Road	Name of Road	Starting Coordinates (Kandawala Sri Lanka)		Ending Coordinates (Kandawala Sri Lanka)		Length of Road (Meters)	Normal Width of Road (Meters)	Developed Width (Meters)
			Left	Right	Left	Right			
14	SG/RWP/A21/8/1	Mudugamuwa 1st Lane Part 02	207601.401/ 144084.556	207600.004/ 144083.957	207596.224/ 144092.222	207595.014/ 144091.301	9.19	1.52	1.52
15	SG/RWP/A21/8/2	Mudugamuwa 1st Lane Part 03	207597.102/ 144092.816	207594.135/ 144090.708	207591.395/ 144124.09	207587.761/ 144123.904	35.62	3.65	3.04
16	SG/RWP/A21/9	Mudugamuwa 2nd Lane	207591.208/ 143879.202	207594.321/ 143882.273	207703.078/ 143845.46	207703.668/ 143849.376	125.72	3.96	3.04
17	SG/RWP/A21/10	Walawwaththa Road	207168.2/ 143605.109	207164.841/ 143602.472	207032.97/ 144082.253	207028.764/ 144082.931	613.67	4.26	3.04
18	SG/RWP/A21/10/1	Walawwaththa Road 1st Lane	207151.17/ 143727.646	207154.238/ 143734.049	207225.355/ 143767.765	207227.888/ 143769.445	102.26	3.04	2.43
19	SG/RWP/A21/10/2	Walawwaththa Road 2nd Lane Part 01	207157.705/ 143821.282	207156.656/ 143817.105	207074.724/ 143850.298	207071.949/ 143847.065	94.12	4.26	2.43
20	SG/RWP/A21/10/2/1	Walawwaththa Road 2nd Lane Part 02	207074.385/ 143850.17	207072.288/ 143847.194	207029.143/ 143873.663	207026.815/ 143870.864	51.62	3.65	2.43
21	SG/RWP/A21/11	Canada Mithra Mawatha	206909.91/ 143512.614	206906.074/ 143511.101	206839.65/ 143911.248	206839.438/ 143905.445	446.5	4.06	3.04
22	SG/RWP/A21/12	Kongahawaththa Kanda Road	206835.48/ 143450.594	206840.009/ 143454.669	206797.934/ 143527.177	206800.04/ 143521.474	184.18	6.09	2.43
23	SG/RWP/A21/13	Anguruwella Kongahawaththa Road	206776.358/ 143405.527	206772.198/ 143402.979	206717.267/ 143456.71	206712.408/ 143456.629	110.67	4.87	3.04
24	SG/RWP/A21/14	Navodya Mawatha (Nawa Udana Mawatha)	206478.673/ 143197.725	206475.765/ 143196.654	206315.558/ 143437.915	206313.215/ 143435.967	325.31	3.04	2.43
25	SG/RWP/A21/14/1	Navodya Mawatha (Nawa Udana Mawatha) 1st Lane	206415.07/ 143312.685	206417.716/ 143307.729	206344.767/ 143320.095	206343.993/ 143316.539	76.94	3.65	3.04
26	SG/RWP/A21/15	Road to Athukorala Mawatha Near Sandya Praja Mandalaya Part 01	206301.487/ 143123.218	206298.747/ 143121.874	206148.156/ 143261.972	206145.594/ 143260.334	240.31	3.04	2.43

Serial No.	Code of Road	Name of Road	Starting Coordinates (Kandawala Sri Lanka)		Ending Coordinates (Kandawala Sri Lanka)		Length of Road (Meters)	Normal Width of Road (Meters)	Developed Width (Meters)
			Left	Right	Left	Right			
27	SG/RWP/A21/15/1	Road to Athukorala Mawatha Near Sandya Praja Mandalaya Part 02	206147.37/ 143261.493	206146.369/ 143260.829	206141.473/ 143270.083	206140.59/ 143269.249	12.63	1.21	1.21
28	SG/RWP/A21/16	Ananda Athukorala Mawatha	205909.999/ 142996.708	205905.092/ 142997.082	206472.425/ 143570.053	206476.049/ 143575.568	823.56	4.57	3.04
29	SG/RWP/A21/16/1	Ananda Athukorala Mawatha 1st Lane	205966.7/ 143096.26	205964.578/ 143093.996	205954.926/ 143216.959	205953.11/ 143219.436	165.48	3.04	2.43
30	SG/RWP/A21/16/2	Ananda Athukorala Mawatha 2nd Lane	205978.445/ 143114.919	205976.753/ 143112.391	205952.914/ 143271.459	205951.457/ 143274.128	187.61	3.04	2.43
31	SG/RWP/A21/16/3	Yatanwala - Ananda Athukorala Mawatha	206047.428/ 143196.201	206043.943/ 143191.948	205860.394/ 143405.294	205858.199/ 143402.389	374.77	3.65	2.74
32	SG/RWP/A21/16/4	Ananda Athukorala Mawatha 3rd Lane	206306.032/ 143435.719	206303.719/ 143433.682	206273.351/ 143495.205	206270.587/ 143493.939	70.75	3.04	2.43
33	SG/RWP/A21/16/5	Ananda Athukorala Mawatha 4th Lane	206344.409/ 143460.193	206346.772/ 143462.157	206390.585/ 143400.843	206393.207/ 143402.382	78.93	3.04	2.43
34	SG/RWP/A21/17	Yatanwala Polwaththa Road	205590.343/ 142928.582	205593.832/ 142929.491	205558.04/ 142861.271	205561.381/ 142861.275	90.61	3.35	3.04
35	SG/RWP/A21/18	Yatanwala Galketiya Road	205591.103/ 142944.308	205586.984/ 142943.201	205537.23/ 143094.105	205534.838/ 143090.581	167.9	4.26	2.74
36	SG/RWP/A21/19	Ruwanwella Thotupola Road	205170.216/ 142628.485	205172.049/ 142631.63	205330.654/ 142525.851	205332.905/ 142528.712	199.31	3.65	2.74
37	SG/RWP/A21/20	Lesly Yatanwala Road	205157.004/ 142635.617	205155.184/ 142632.465	204905.065/ 142596.033	204910.357/ 142594.684	321.84	3.65	3.04
38	SG/RWP/A21/20/1	Lesly Yatanwala Road 1st Lane	205011.282/ 142684.538	205009.049/ 142683.559	205000.312/ 142781.472	204997.972/ 142782.092	124.39	2.43	3.65
39	SG/RWP/A21/21	Ruwanwella Police Station Road	205143.752/ 142607.141	205140.895/ 142603.836	205077.71/ 142621.013	205078.268/ 142616.789	73.61	4.26	3.04

Serial No.	Code of Road	Name of Road	Starting Coordinates (Kandawala Sri Lanka)		Ending Coordinates (Kandawala Sri Lanka)		Length of Road (Meters)	Normal Width of Road (Meters)	Developed Width (Meters)
			Left	Right	Left	Right			
40	SG/RWP/A21/22	Ruwanwella Sathosa Road	204825.015/ 142619.933	204820.924/ 142621.183	204826.786/ 142691.526	204822.612/ 142690.671	77.39	4.26	3.04
41	SG/RWP/A21/23	Ruwanwella Public Ground Road	204798.149/ 142615.553	204804.659/ 142613.448	205013.59/ 142473.801	205006.571/ 142474.959	540.85	6.7	3.65
42	SG/RWP/A21/23/1	Ruwanwella Public Ground Road 1st Lane	204806.626/ 142504.866	204806.76/ 142511.566	205019.344/ 142474.051	205018.103/ 142480.642	229.46	6.7	6.09
43	SG/RWP/A21/24	Road Near Ruwanwella Mosque	204667.24/ 142681.053	204668.586/ 142677.206	204449.865/ 142647.802	204453.11/ 142646.154	246.94	3.65	2.43
44	SG/RWP/A21/25	Kesel Kotuwa Waththa Road	204675.184/ 142772.514	204672.128/ 142775.575	204657.628/ 142859.602	204655.439/ 142856.301	109.67	3.96	2.74
45	SG/RWP/A21/26	Road Near Playground of Rajasingha School Part 01	204417.915/ 142838.304	204423.402/ 142837.47	204405.504/ 142814.072	204409.402/ 142810.22	35.66	5.48	4.87
46	SG/RWP/A21/26/1	Ruwanwella Central Library Road	204415.691/ 142829.71	204414.467/ 142825.476	204370.198/ 142833.54	204369.831/ 142829.296	48.08	4.26	3.04
47	SG/RWP/A21/26/2	Road Near Playground of Rajasingha School Part 02	204406.443/ 142813.281	204408.464/ 142811.01	204357.997/ 142668.831	204359.783/ 142671.29	245.4	3.04	2.43
48	SG/RWP/A21/26/2/1	Road Near Playground of Rajasingha School 1st Lane	204303.673/ 142753.393	204302.72/ 142751.832	204236.368/ 142772.944	204235.427/ 142771.316	76.52	1.82	1.82
49	SG/RWP/A21/26/2/2	Road Near Playground of Rajasingha School 2nd Lane	204333.432/ 142685.539	204335.25/ 142683.079	204296.081/ 142577.246	204299.075/ 142576.718	119.84	3.04	2.43
50	SG/RWP/A21/26/3	Road Near Playground of Rajasingha School Part 03	204358.33/ 142669.343	204359.45/ 142670.778	204398.703/ 142600.852	204400.386/ 142601.546	83.73	1.82	1.82
51	SG/RWP/A21/27	Medigodalla Road	204289.508/ 142902.662	204285.896/ 142902.163	204249.576/ 143083.256	204249.635/ 143086.895	365.77	3.65	2.43
52	SG/RWP/A21/27/1	Medigodalla Road 1st Lane	204207.493/ 142971.052	204204.577/ 142972.754	204200.528/ 143004.438	204197.893/ 143003.689	35.25	2.74	2.43
53	SG/RWP/A21/27/2	Medigodalla Road 2nd Lane	204163.857/ 143001.224	204165.405/ 142998.369	204127.128/ 143007.44	204126.393/ 143004.801	40.62	2.74	2.43
54	SG/RWP/A21/28	Road Near Water Supply Board Ruwanwella	204236.822/ 142865.293	204235.382/ 142862.225	204173.523/ 142930.293	204171.399/ 142927.715	112.75	3.35	2.43
55	SG/RWP/A21/29	Kahatagasthenna 1st Lane	204210.181/ 142753.186	204213.741/ 142753.964	204170.884/ 142716.108	204173.459/ 142713.535	77.42	3.65	3.04

Serial No.	Code of Road	Name of Road	Starting Coordinates (Kandawala Sri Lanka)		Ending Coordinates (Kandawala Sri Lanka)		Length of Road (Meters)	Normal Width of Road (Meters)	Developed Width (Meters)
			Left	Right	Left	Right			
56	SG/RWP/A21/29/1	Kahatagastanna 1st Lane Bypass Road	204211.909/ 142720.695	204214.506/ 142724.457	204260.139/ 142734.883	204257.965/ 142737.803	51.03	3.65	3.04
57	SG/RWP/A21/30	Kahatagastanna 2nd Lane	204133.453/ 142777.787	204135.121/ 142776.96	204118.124/ 142737.512	204119.92/ 142737.809	49.48	1.82	1.82
58	SG/RWP/A21/31	Kahatagastanna 3rd Lane	204063.164/ 142832.794	204061.281/ 142833.789	204102.904/ 142889.304	204101.582/ 142890.962	89.75	2.13	1.82
59	SG/RWP/A21/32	Petigahamula Road	204023.154/ 142839.944	204024.768/ 142839.083	203971.418/ 142704.064	203973.045/ 142703.249	151.76	1.82	1.82
60	SG/RWP/A21/33	Kossinage Mawatha	203991.257/ 142871.047	203988.575/ 142872.481	204067.38/ 143041.946	204064.525/ 143042.992	233.35	3.04	2.43
61	SG/RWP/A21/34	Ebawaththa Road Part 01	203953.08/ 142887.915	203949.616/ 142889.15	204105.835/ 143130.874	204102.199/ 143131.044	357.25	3.65	2.74
62	SG/RWP/A21/34/1	Ebawaththa Road 1st Lane	204001.319/ 143084.607	203999.489/ 143082.036	203925.148/ 143166.44	203922.119/ 143166.704	144.92	3.04	2.43
63	SG/RWP/A21/34/1/1	Ebawaththa Road 1st Lane 1st Bypass Road	203968.653/ 143096.807	203965.815/ 143097.918	203993.855/ 143171.189	203991.644/ 143173.275	81.45	3.04	2.43
64	SG/RWP/A21/34/2	Ebawaththa Road 2nd Lane	204014.25/ 143084.914	204011.215/ 143085.108	204029.817/ 143146.469	204026.874/ 143147.23	65.64	3.04	2.43
65	SG/RWP/A21/34/3	Ebawaththa Road 3rd Lane	204041.348/ 143091.271	204038.021/ 143089.424	204053.442/ 143145.708	204050.429/ 143146.116	59.31	3.04	2.43
66	SG/RWP/A21/34/4	Ebawaththa Road Part 02	204104.618/ 143130.931	204103.421/ 143131.028	204111.123/ 143186.537	204109.927/ 143186.622	56.08	1.21	1.21
67	SG/RWP/A21/35	Gangabadawaththa Thotupala Road Part 01	203786.639/ 142942.285	203790.025/ 142940.442	203786.989/ 142759.63	203788.814/ 142756.48	223.05	3.65	2.74
68	SG/RWP/A21/35/1	Gangabadawaththa Thotupala Road 1st Lane	203783.139/ 142896.171	203783.165/ 142892.447	203751.335/ 142835.633	203754.887/ 142834.841	72.16	3.65	3.04
69	SG/RWP/A21/35/2	Gangabadawaththa Thotupala Road Part 02	203787.604/ 142758.575	203788.199/ 142757.534	203772.634/ 142750.023	203773.23/ 142748.981	17.24	1.21	1.21
70	SG/RWP/A21/36	Samangi Mawatha	203775.606/ 142961.673	203771.593/ 142963.84	203810.734/ 143136.881	203806.371/ 143138.208	185.44	4.57	3.04
71	SG/RWP/A21/36/1	Victor Jayasooriya Mawatha	203782.144/ 142991.096	203781.936/ 142995.286	203877.121/ 143048.796	203873.853/ 143050.398	147.22	3.65	3.04


Serial No.	Code of Road	Name of Road	Starting Coordinates (Kandawala Sri Lanka)		Ending Coordinates (Kandawala Sri Lanka)		Length of Road (Meters)	Normal Width of Road (Meters)	Developed Width (Meters)
			Left	Right	Left	Right			
72	SG/RWP/A21/37	Wendala 1st Lane	203724.298/ 142974.933	203727.011/ 142973.555	203687.585/ 142868.411	203690.484/ 142867.497	118.53	3.04	2.43
73	SG/RWP/A21/38	Wendala Kehel Baddala Road Part 01	203595.62/ 143018.061	203592.033/ 143017.39	204708.379/ 144020.327	204708.862/ 144023.935	1839.61	3.65	3.04
74	SG/RWP/A21/38/1	Wendala Kehel Baddala Road 1st Lane	203613.416/ 143182.411	203613.135/ 143180.006	203507.804/ 143211.192	203506.134/ 143212.943	129.77	2.43	2.43
75	SG/RWP/A21/38/2	Kiriwana Road	203625.536/ 143400.884	203625.989/ 143405.725	204512.36/ 143142.892	204516.461/ 143145.998	1050.12	4.87	3.04
76	SG/RWP/A21/38/2/1	Kiriwana Road 1st Lane	203781.132/ 143354.749	203776.769/ 143357.021	203800.603/ 143429.578	203796.556/ 143432.268	80.76	4.87	2.43
77	SG/RWP/A21/38/2/2	Kiriwana Road 2nd Lane	203942.418/ 143300.509	203939.473/ 143301.302	204041.119/ 143514.191	204038.192/ 143515.21	272.08	3.04	2.43
78	SG/RWP/A21/38/2/3	Kiriwana Road 3rd Lane	204077.915/ 143267.443	204079.15/ 143271.528	204156.444/ 143252.219	204157.055/ 143256.436	82.15	4.87	3.04
79	SG/RWP/A21/38/2/4	Kiriwana Waththa Road	204157.959/ 143336.98	204154.772/ 143336.494	203662.898/ 143576.788	203660.78/ 143574.549	655.82	3.04	2.43
80	SG/RWP/A21/38/2/4/1	Kiriwanwaththa Road 1st Lane	204120.052/ 143462.384	204120.217/ 143466.02	204179.395/ 143537.112	204175.871/ 143538.022	118.05	3.65	2.43
81	SG/RWP/A21/38/2/5	Kiriwana Road 4th Lane	204348.844/ 143297.431	204346.544/ 143301.796	204333.874/ 143524.902	204334.623/ 143521.955	269.4	3.04	2.43
82	SG/RWP/A21/38/3	K.R. Gunasekara Mawatha	203621.408/ 143416.222	203621.942/ 143411.578	202907.324/ 143337.844	202911.053/ 143335.771	832.3	4.26	3.04
83	SG/RWP/A21/38/3/1	Wendala Dewala Road	203243.57/ 143485.002	203239.936/ 143488.284	203106.019/ 143741.448	203101.915/ 143738.842	387.89	4.87	3.04
84	SG/RWP/A21/38/3/1/1	Pasal Mawatha	203293.174/ 143546.88	203292.961/ 143550.518	203624.86/ 143552.222	203627.281/ 143554.985	367.83	3.65	2.74
85	SG/RWP/A21/38/4	Sulico Road	203623.078/ 143463.454	203622.855/ 143468.021	203785.24/ 143495.121	203787.172/ 143499.252	176.28	4.57	2.43
86	SG/RWP/A21/38/5	Annasi Kotuwa Road	203716.369/ 143688.692	203714.939/ 143686.639	203598.838/ 143737.97	203599.812/ 143735.755	155.69	2.43	2.43
87	SG/RWP/A21/38/6	Wendala Kehel Baddala Road 2nd Lane	203746.209/ 143728.245	203747.479/ 143730.311	203793.658/ 143646.014	203795.815/ 143647.114	98.13	2.43	2.43


Serial No.	Code of Road	Name of Road	Starting Coordinates (Kandawala Sri Lanka)		Ending Coordinates (Kandawala Sri Lanka)		Length of Road (Meters)	Normal Width of Road (Meters)	Developed Width (Meters)
			Left	Right	Left	Right			
88	SG/RWP/A21/38/7	Wendala Kehel Baddala Road Part 02	204708.419/ 144020.628	204708.825/ 144023.641	205031.51/ 144334.11	205029.934/ 144336.712	515.2	3.04	2.43
89	SG/RWP/A21/39	Miyanapalawa Road Part 01	203478.826/ 143010.115	203482.45/ 143009.778	203490.224/ 142802.211	203493.825/ 142802.739	213.75	3.65	3.04
90	SG/RWP/A21/39/1	Miyanapalawa Road 1st Lane	203486.291/ 142905.232	203486.285/ 142902.658	203396.615/ 142991.851	203394.194/ 142991.961	160.56	2.43	2.43
91	SG/RWP/A21/39/2	Miyanapalawa Road 2nd Lane	203490.345/ 142843.798	203489.954/ 142840.043	203304.927/ 142896.351	203302.981/ 142893.275	198.71	3.65	2.43
92	SG/RWP/A21/39/3	Miyanapalawa Road Part 02	203490.828/ 142802.3	203493.223/ 142802.64	203493.141/ 142787.77	203495.53/ 142788.154	14.7	2.43	1.82
93	SG/RWP/A21/40	Balahena Road	203470.163/ 143022.428	203465.239/ 143022.342	203392.027/ 143184.183	203393.249/ 143188.265	24.94	3.65	2.43
94	SG/RWP/A21/41	Kahatagasthenna Bala Hena Road	203442.728/ 143018.987	203434.935/ 143016.135	203458.887/ 143034.87	203456.706/ 143031.81	354.3	4.26	3.04
95	SG/RWP/A21/42	Pahalamulla Road Part 01	203298.628/ 143040.843	203306.471/ 143037.455	202906.49/ 143205.188	202904.047/ 143202.487	716.23	3.65	2.43
96	SG/RWP/A21/42/1	School Ground Road Part 01	203156.507/ 142956.714	203151.713/ 142955.282	203134.087/ 143019.626	203131.057/ 143019.379	72.48	3.04	2.43
97	SG/RWP/ A21/42/1/1	School Ground Road Part 02	203133.48/ 143019.577	203131.663/ 143019.459	203152.287/ 143104.019	203150.802/ 143105.09	135.87	1.82	1.82
98	SG/RWP/A21/42/2	Pahalamulla Road 1st Lane	202868.023/ 143059.099	202876.144/ 143055.631	202758.796/ 143074.863	202760.213/ 143072.173	129.73	3.04	2.43
99	SG/RWP/A21/42/3	Pahalamulla Road Part 02	202906.802/ 143205.728	202903.654/ 143202.025	202772.475/ 143347.365	202767.592/ 143347.722	216.23	4.87	3.65
100	SG/RWP/ A21/42/3/1	Maligawaththa Road Part 01	202777.678/ 143296.009	202780.245/ 143292.101	202477.717/ 143159.714	202480.699/ 143158.208	387.8	3.35	2.43
101	SG/RWP/ A21/42/3/1/1	Maligawaththa Road 1st Lane	202603.997/ 143186.592	202606.94/ 143185.809	202553.535/ 143068.226	202556.574/ 143068.183	147.64	3.04	2.43
102	SG/RWP/ A21/42/3/1/2	Maligawaththa Road Part 02	202478.104/ 143159.458	202480.288/ 143158.416	202441.978/ 143079.266	202444.185/ 143078.273	87.96	2.43	1.82


Serial No.	Code of Road	Name of Road	Starting Coordinates (Kandawala Sri Lanka)		Ending Coordinates (Kandawala Sri Lanka)		Length of Road (Meters)	Normal Width of Road (Meters)	Developed Width (Meters)
			Left	Right	Left	Right			
103	SG/RWP/A21/43	Road Near Electricity Board	203055.79/ 143214.585	203057.914/ 143210.353	202947.634/ 143121.99	202951.617/ 143120.479	183.32	4.26	3.04
104	SG/RWP/A21/44	Daham Mawatha	202851.29/ 143351.633	202847.654/ 143351.789	202872.36/ 143447.796	202869.093/ 143449.4	106.39	3.65	2.43
105	SG/RWP/A21/ C612/1	Yatanwala Karawdeniya Kanda Road	206595.819/ 143655.703	206592.633/ 143653.929	204706.416/ 143297.18	204711.071/ 143296.441	2363.99	3.65	2.43
106	SG/RWP/A21/ C612/1/1	Yatanwala Karawdeniya Kanda Road 1st Lane	206344.588/ 143756.152	206346.115/ 143753.537	206318.351/ 143695.516	206320.804/ 143697.312	88.1	3.04	2.43
107	SG/RWP/A21/ C612/1/2	Yatanwala Karawdeniya Kanda Road 2nd Lane	206283.457/ 143801.381	206279.885/ 143800.481	206272.199/ 143865.425	206268.986/ 143867.135	69.16	3.65	2.13
108	SG/RWP/A21/ C612/1/3	Yatanwala Karawdeniya Kanda Road 3rd Lane	205898.584/ 143627.089	205904.496/ 143628.509	205258.541/ 143129.005	205261.288/ 143123.557	993.27	6.09	3.04
109	SG/RWP/A21/ C612/1/3/1	Yatanwala Karawdeniya Kanda Road 3rd Lane 1st Bypass Road	205920.647/ 143521.772	205921.045/ 143526.866	205955.998/ 143467.391	205960.191/ 143468.142	81.98	4.26	3.04
110	SG/RWP/A21/ C612/1/3/2	Yatanwala Karawdeniya Kanda Road 3rd Lane 2nd Bypass Road	205830.053/ 143406.2	205826.324/ 143408.304	205810.303/ 143456.874	205809.53/ 143453.317	68.7	3.65	2.43
111	SG/RWP/A21/ C612/1/3/3	Yatanwala Karawdeniya Kanda Road 3rd Lane 3rd Bypass Road	205766.953/ 143320.693	205770.807/ 143322.596	205841.099/ 143302.189	205837.928/ 143303.977	90.09	3.65	2.43
112	SG/RWP/A21/ C612/1/3/4	Yatanwala Karawdeniya Kanda Road 3rd Lane 4th Bypass Road	205553.287/ 143246.447	205549.906/ 143244.821	205571.687/ 143316.289	205568.084/ 143316.805	76.92	3.65	3.04
113	SG/RWP/A21/ C612/1/3/5	Yatanwala Karawdeniya Kanda Road 3rd Lane 5th Bypass Road	205426.259/ 143229.245	205422.064/ 143229.311	205402.954/ 143323.969	205398.695/ 143323.926	109.46	4.26	2.74
114	SG/RWP/A21/ C612/1/3/6	Yatanwala Karawdeniya Kanda Road 3rd Lane 6th Bypass Road	205284.389/ 143147.623	205280.263/ 143145.337	205318.517/ 143246.756	205314.259/ 143246.821	119.26	4.26	2.74


Serial No.	Code of Road	Name of Road	Starting Coordinates (Kandawala Sri Lanka)		Ending Coordinates (Kandawala Sri Lanka)		Length of Road (Meters)	Normal Width of Road (Meters)	Developed Width (Meters)
			Left	Right	Left	Right			
115	SG/RWP/A21/ C612/1/4	Yatanwala Karawdeniya Kanda Road 4th Lane	205566.654/ 143648.297	205564.45/ 143645.097	205318.583/ 143876.307	205315.415/ 143874.516	446.76	3.65	2.74
116	SG/RWP/A21/ C612/1/5	Yatanwala Karawdeniya Kanda Road 5th Lane	205453.672/ 143602.565	205449.321/ 143601.677	205106.299/ 143818.729	205102.315/ 143817.219	440.27	4.26	2.43
117	SG/RWP/A21/ C612/2	Anguruwella Galpatha Road 1st Lane	206681.503/ 143715.765	206683.02/ 143718.069	206709.381/ 143677.729	206711.768/ 143679.073	53.71	2.74	2.13
118	SG/RWP/A21/ C612/3	Anguruwella Galpatha Road 2nd Lane	206727.207/ 143780.97	206729.333/ 143783.146	206784.168/ 143719.498	206786.458/ 143721.496	86.99	3.04	2.43
119	SG/RWP/A21/ C612/4	Galpatha Indigolla Road	206731.115/ 143793.582	206728.992/ 143791.407	206686.807/ 143889.212	206684.142/ 143887.75	109.86	3.04	2.43
120	SG/RWP/A21/ C612/5	Anguruwella Galpatha Road 3rd Lane	206743.851/ 143798.147	206745.946/ 143800.357	206780.731/ 143757.864	206783.07/ 143759.805	57.87	3.04	2.43
121	SG/RWP/A21/ C612/6	Doranuwa Temple Road	206836.848/ 143918.808	206833.524/ 143922.929	206557.553/ 144182.398	206560.589/ 144178.504	753.3	4.87	3.65
122	SG/RWP/A21/ C612/6/1	Cemetery Road Near Doranuwa Temple	206822.123/ 144315.196	206819.475/ 144316.731	206842.959/ 144416.832	206839.99/ 144417.487	107.72	3.04	2.43
123	SG/RWP/A21/ C612/7	Paranawaththa Road	206635.228/ 144078.759	206632.858/ 144081.658	206661.131/ 144131.375	206657.642/ 144132.412	80.74	3.65	3.04
124	SG/RWP/A21/ C612/8	Shramashakthi Mawatha	206522.635/ 144203.718	206526.652/ 144200.666	206009.469/ 143935.006	206012.312/ 143931.064	637.66	4.87	3.04
125	SG/RWP/A21/ D605/1	Welikada Road	205259.797/ 142969.429	205259.509/ 142965.793	204858.506/ 143183.131	204854.868/ 143183.035	529.33	3.65	2.74
126	SG/RWP/A21/ D605/1/1	Wellikada Road 1st Lane	205102.469/ 142967.065	205098.291/ 142967.318	204987.87/ 143052.083	204984.861/ 143050.035	160.24	3.65	2.43
127	SG/RWP/A21/ D605/2	Yatanwala Kanda Road 1st Lane	205270.745/ 143068.745	205272.29/ 143064.794	205193.086/ 143102.49	205191.288/ 143099.325	90.1	3.65	2.43
128	SG/RWP/A21/ D605/3	Yatanwala Kanda Road 2nd Lane	205216.458/ 143163.751	205213.434/ 143164.227	205261.803/ 143307.76	205260.158/ 143310.317	158.84	3.04	2.43
129	SG/RWP/A21/ D605/4	Yatanwala Kanda Road 3rd Lane	205115.185/ 143167.818	205111.558/ 143168.563	205117.368/ 143289.463	205113.728/ 143289.53	125.12	3.65	2.43


Serial No.	Code of Road	Name of Road	Starting Coordinates (Kandawala Sri Lanka)		Ending Coordinates (Kandawala Sri Lanka)		Length of Road (Meters)	Normal Width of Road (Meters)	Developed Width (Meters)
			Left	Right	Left	Right			
130	SG/RWP/A21/D605/5	Yatanwala Kanda Road 4th Lane	204664.465/ 143296.572	204659.938/ 143295.988	204495.61/ 143449.279	204494.826/ 143444.787	285.84	4.57	2.43
131	SG/RWP/A21/D605/6	Yatanwala Kanda Road 5th Lane	204496.093/ 143032.908	204498.329/ 143030.017	204327.584/ 143059.814	204327.035/ 143056.215	191.72	3.65	2.74
132	SG/RWP/A07/1	Karawanella Thotupola Road	202385.588/ 143397.394	202392.979/ 143392.322	202199.024/ 143475.458	202198.814/ 143471.824	227.96	3.65	2.43
133	SG/RWP/A07/1/1	Pitiya Road	202301.006/ 143420.456	202304.554/ 143419.357	202147.224/ 143129.688	202147.407/ 143126.053	368.1	3.65	2.43
134	SG/RWP/A07/1/1/1	Pitiya Road 1st Lane	202255.839/ 143247.163	202255.216/ 143243.869	202198.866/ 143236.762	202199.075/ 143233.429	64.82	3.35	2.43

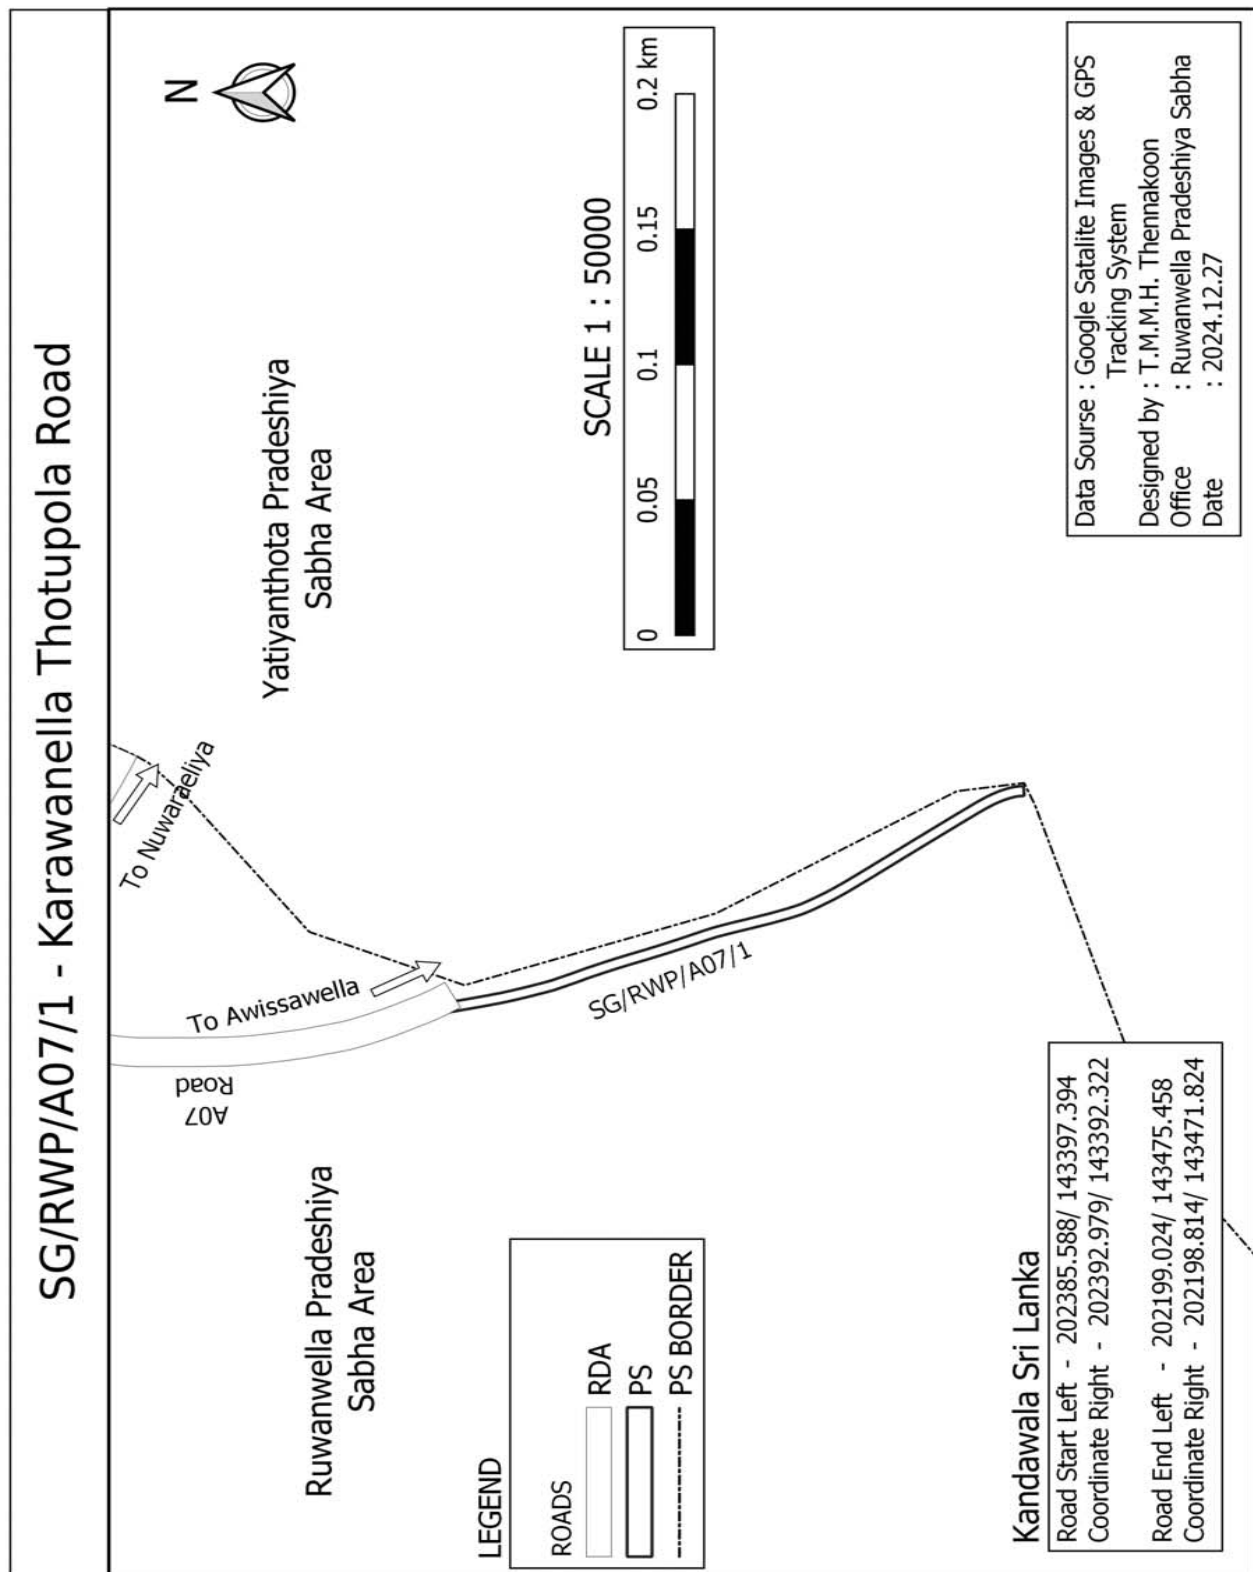


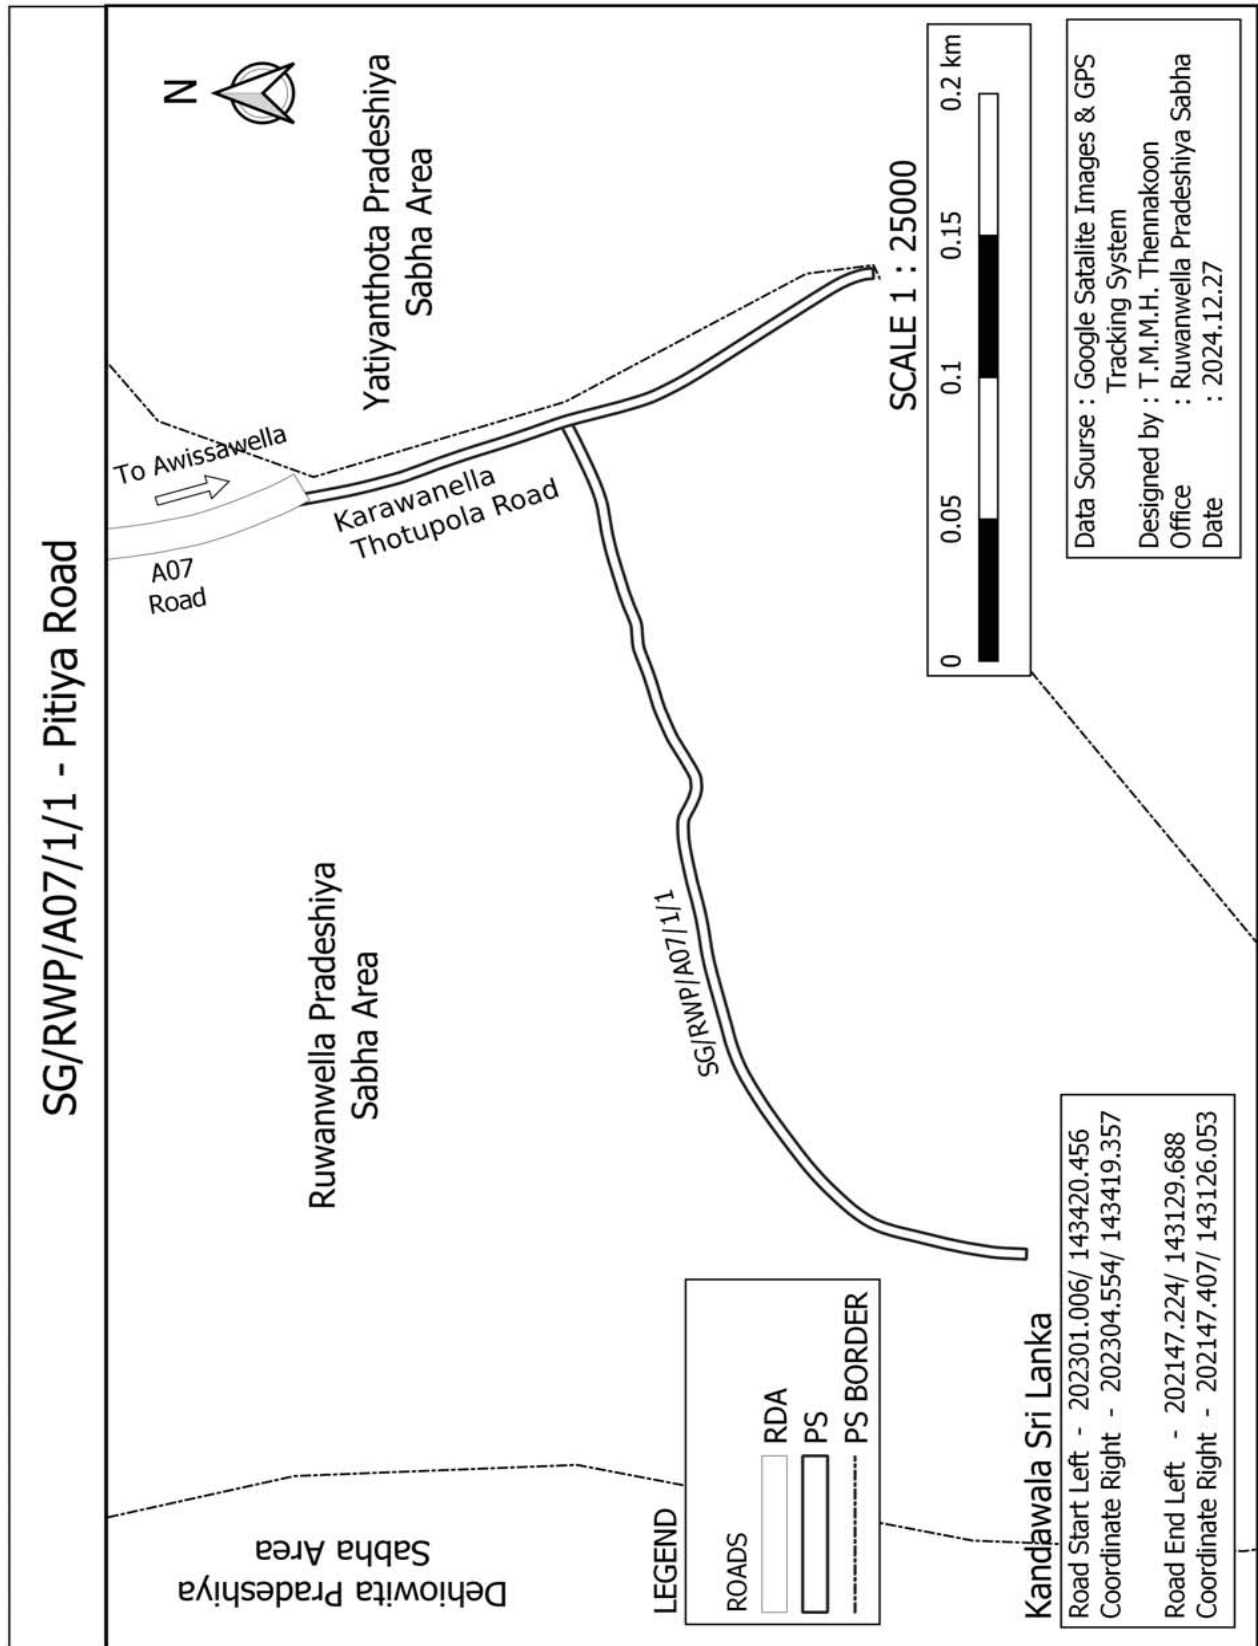


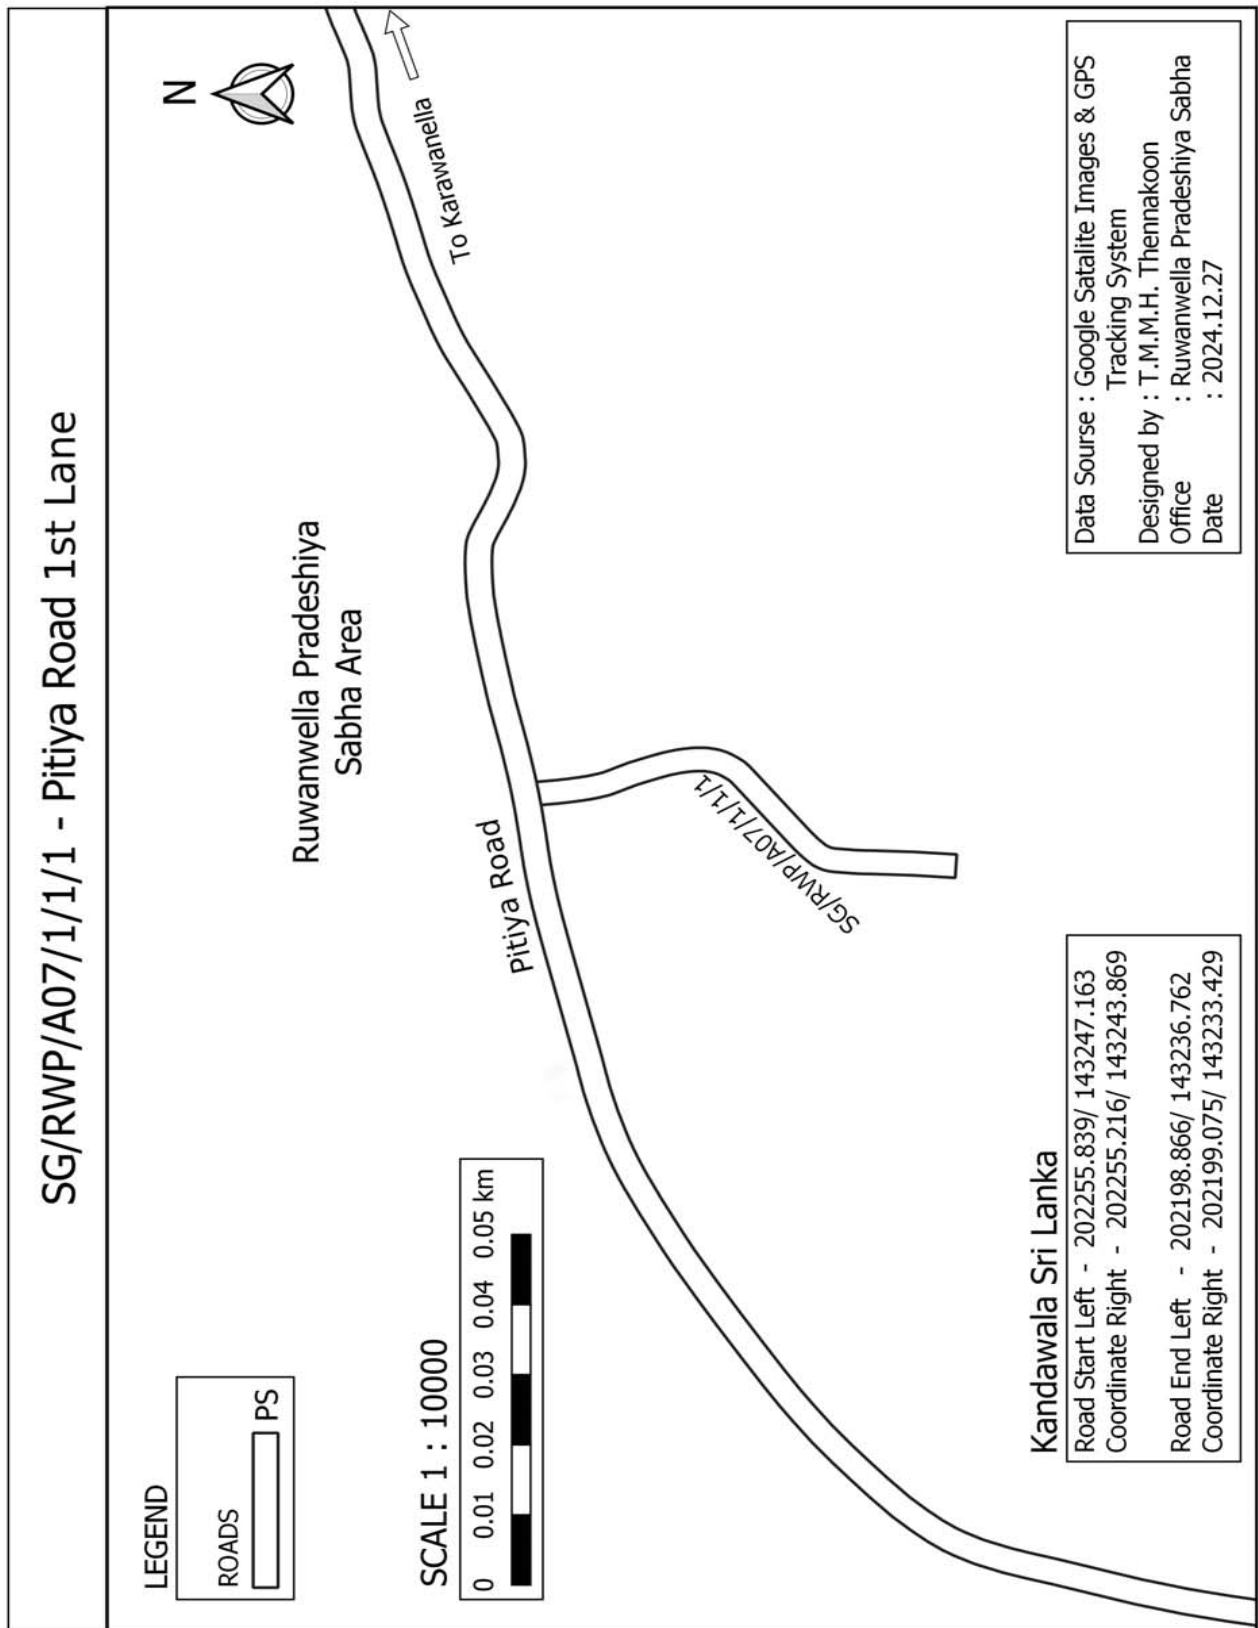


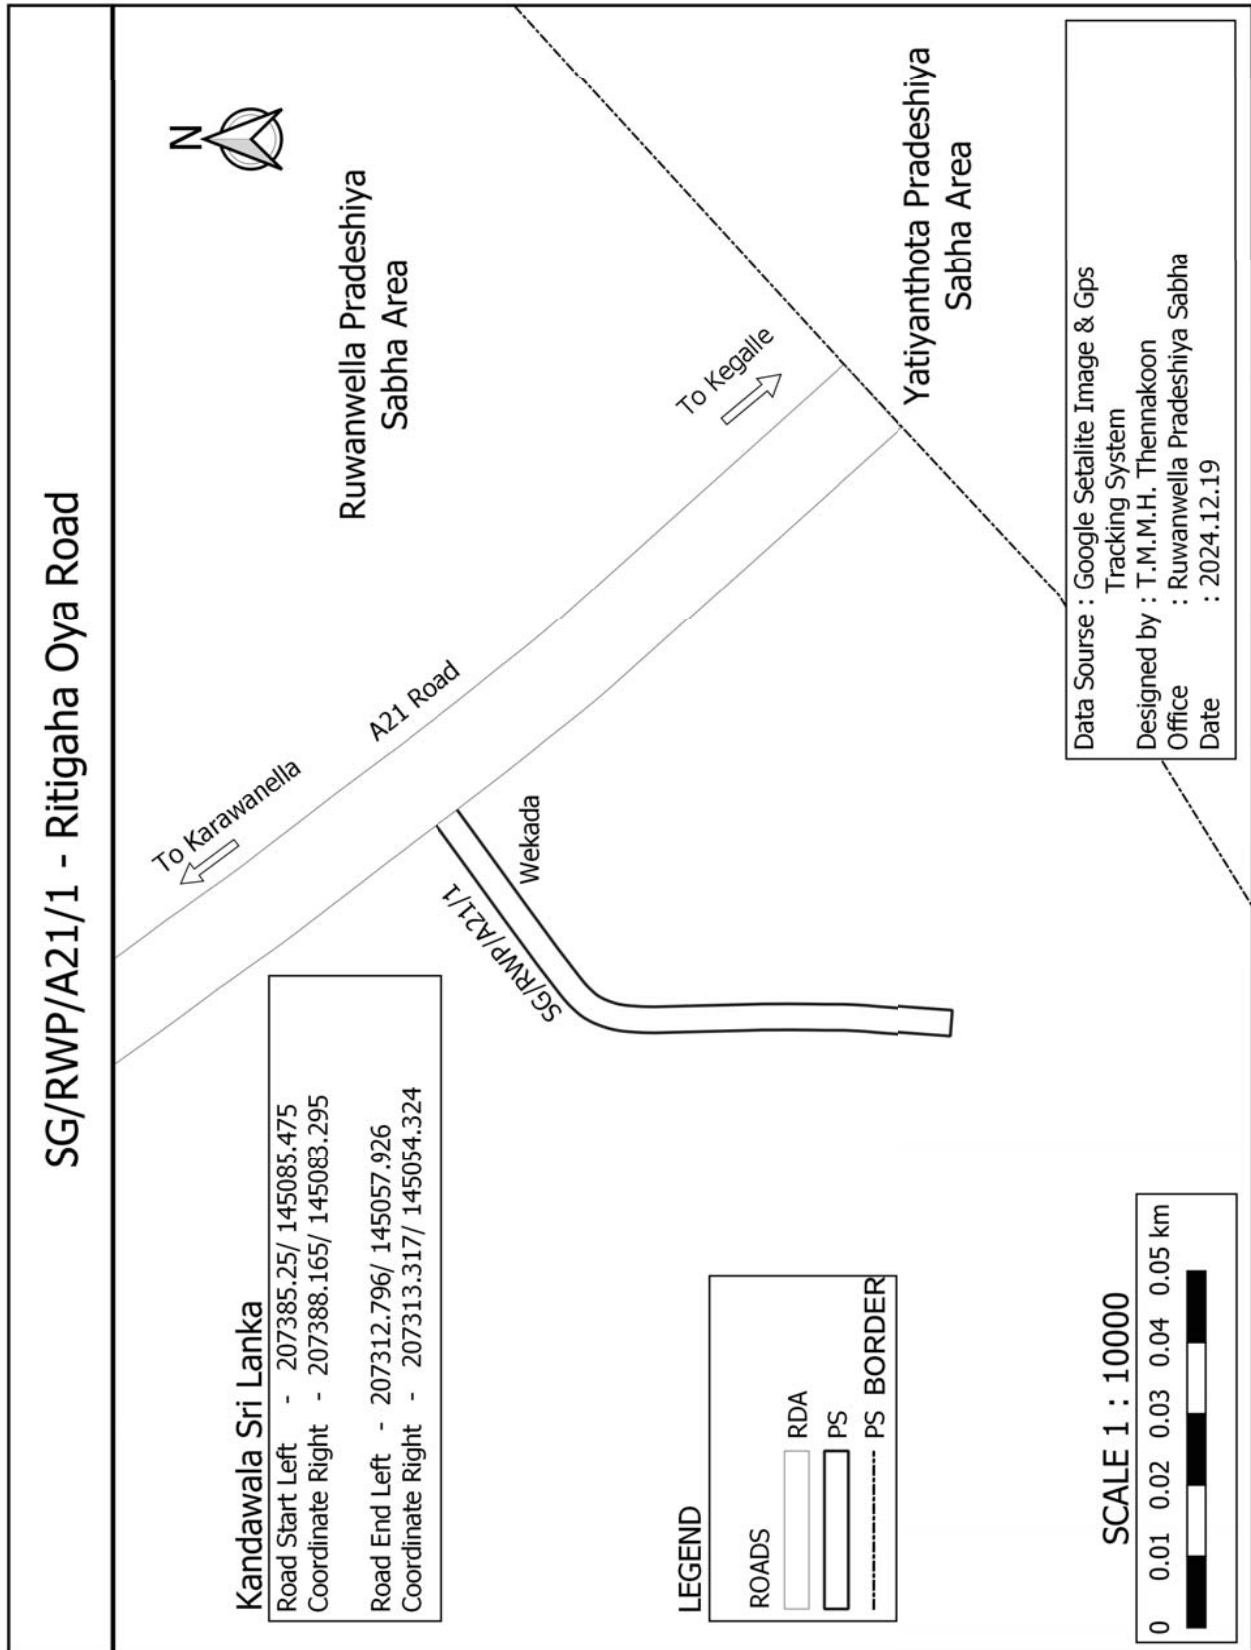


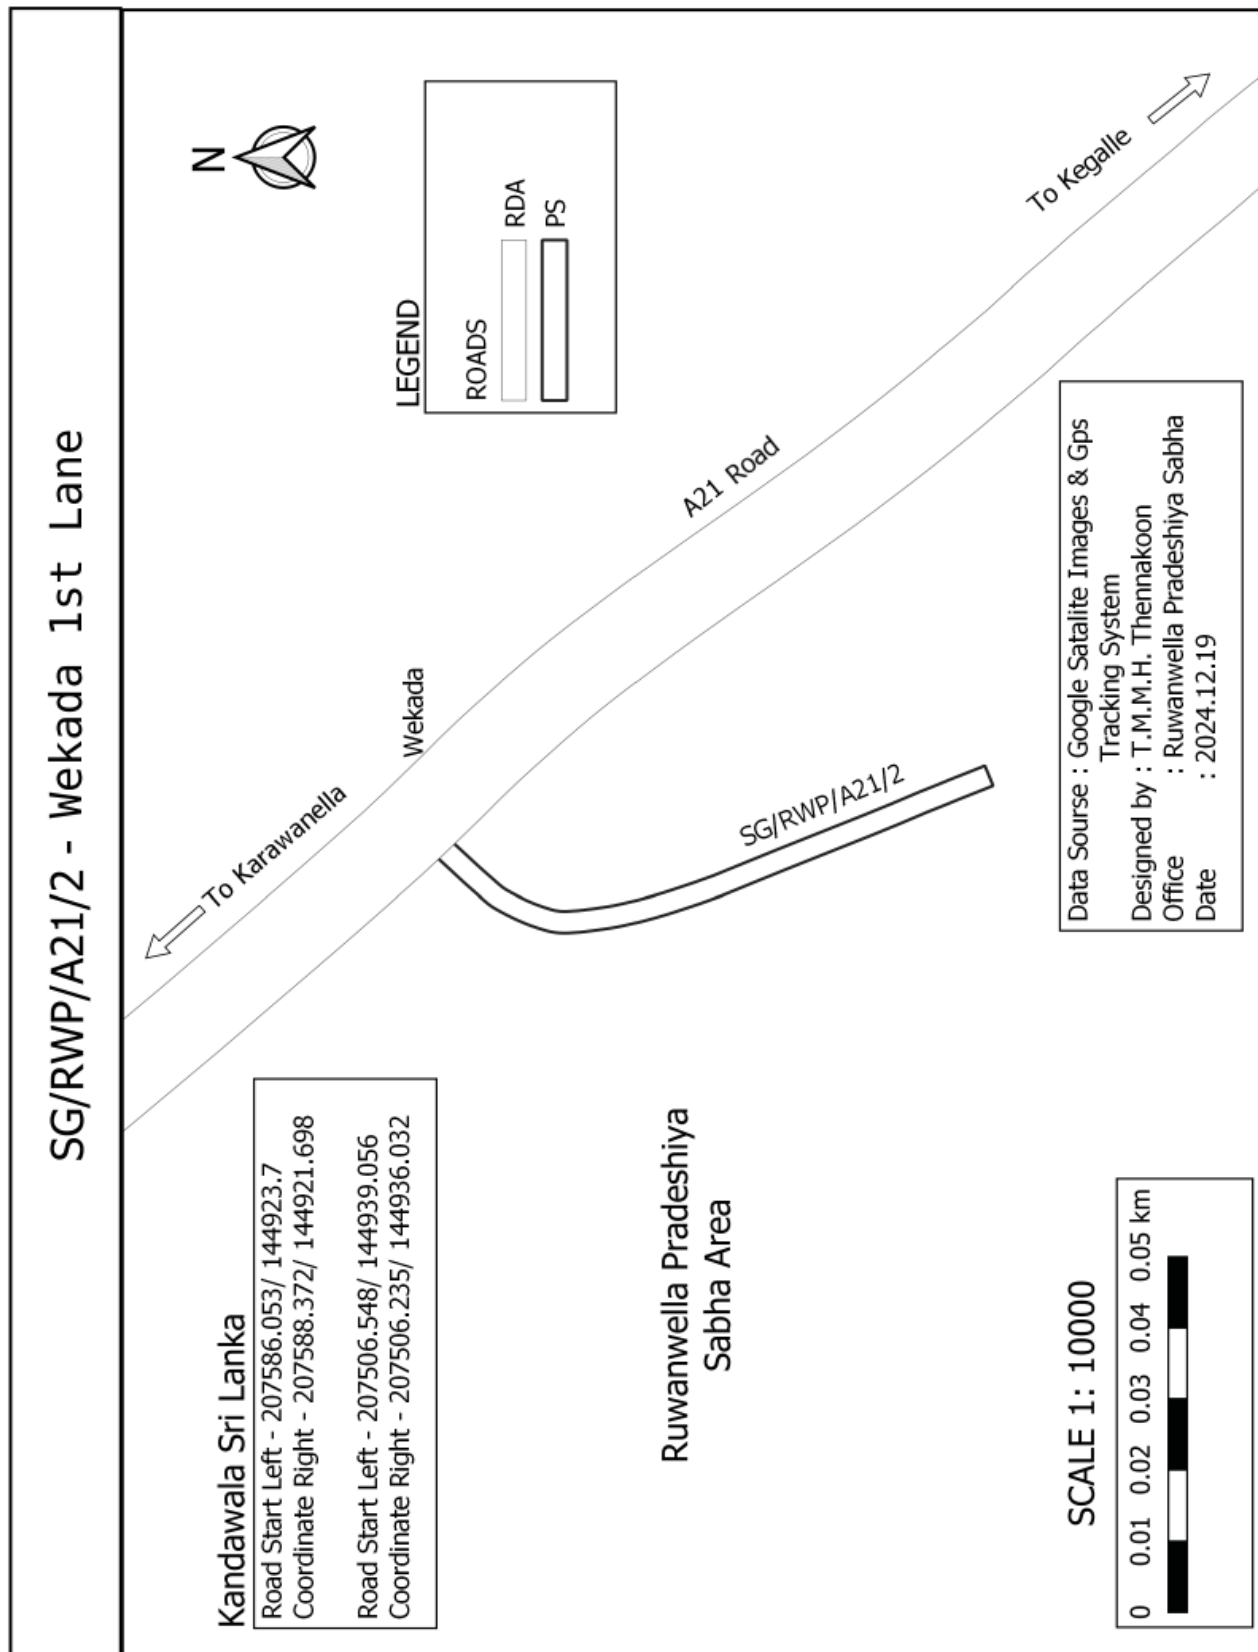


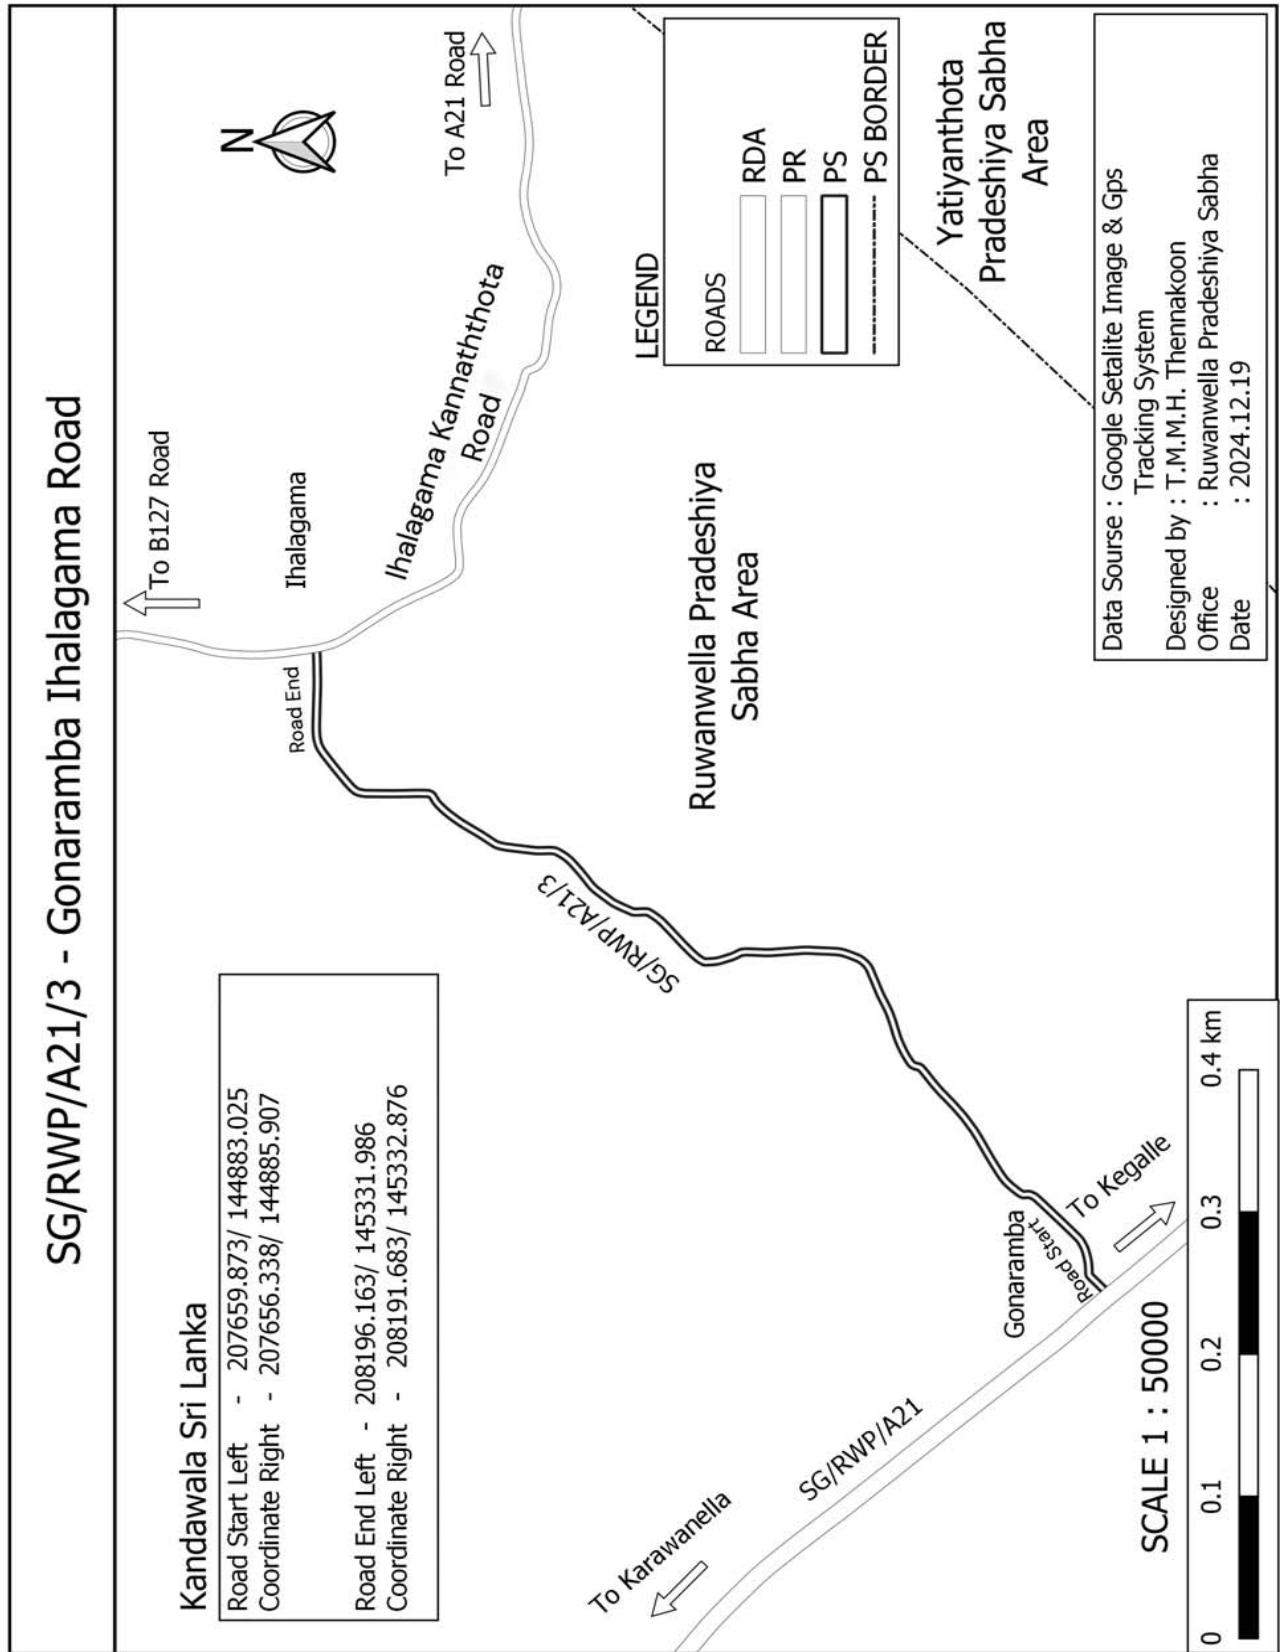


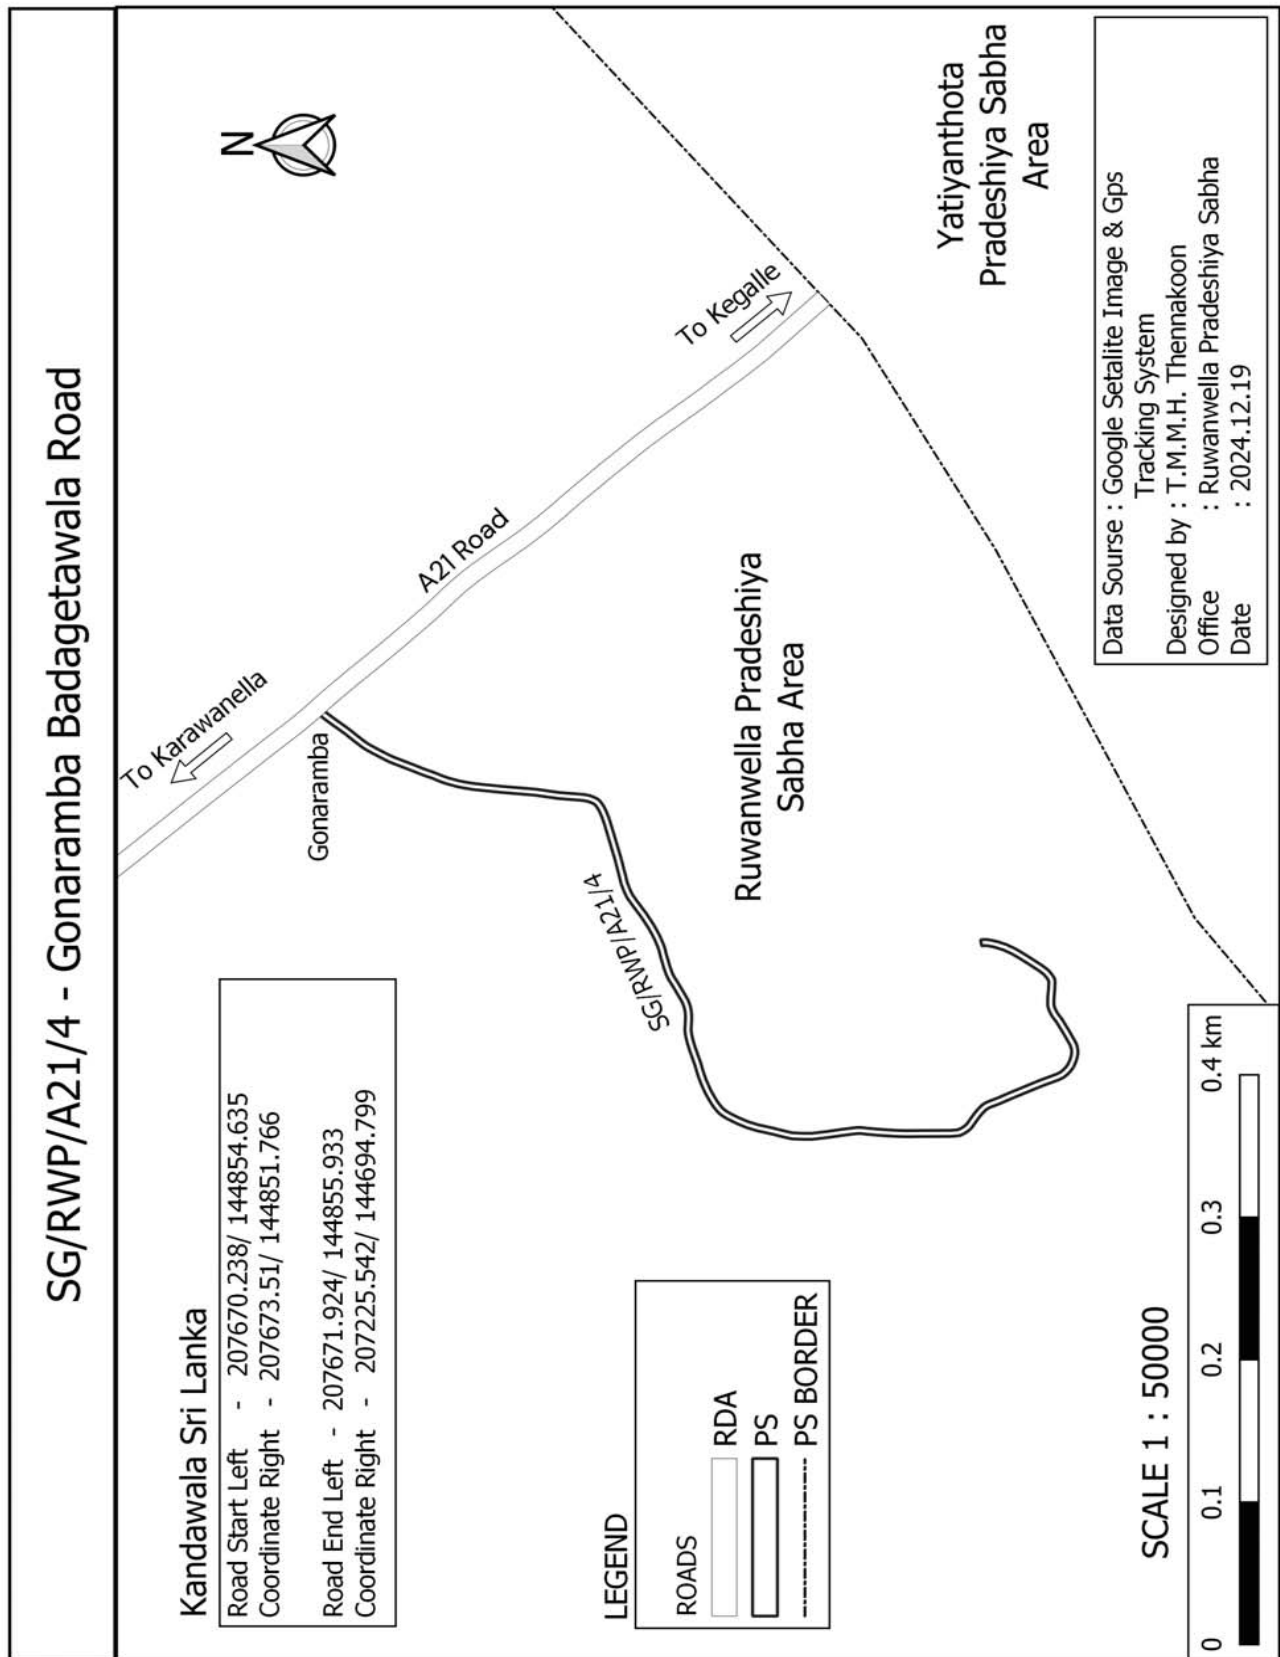


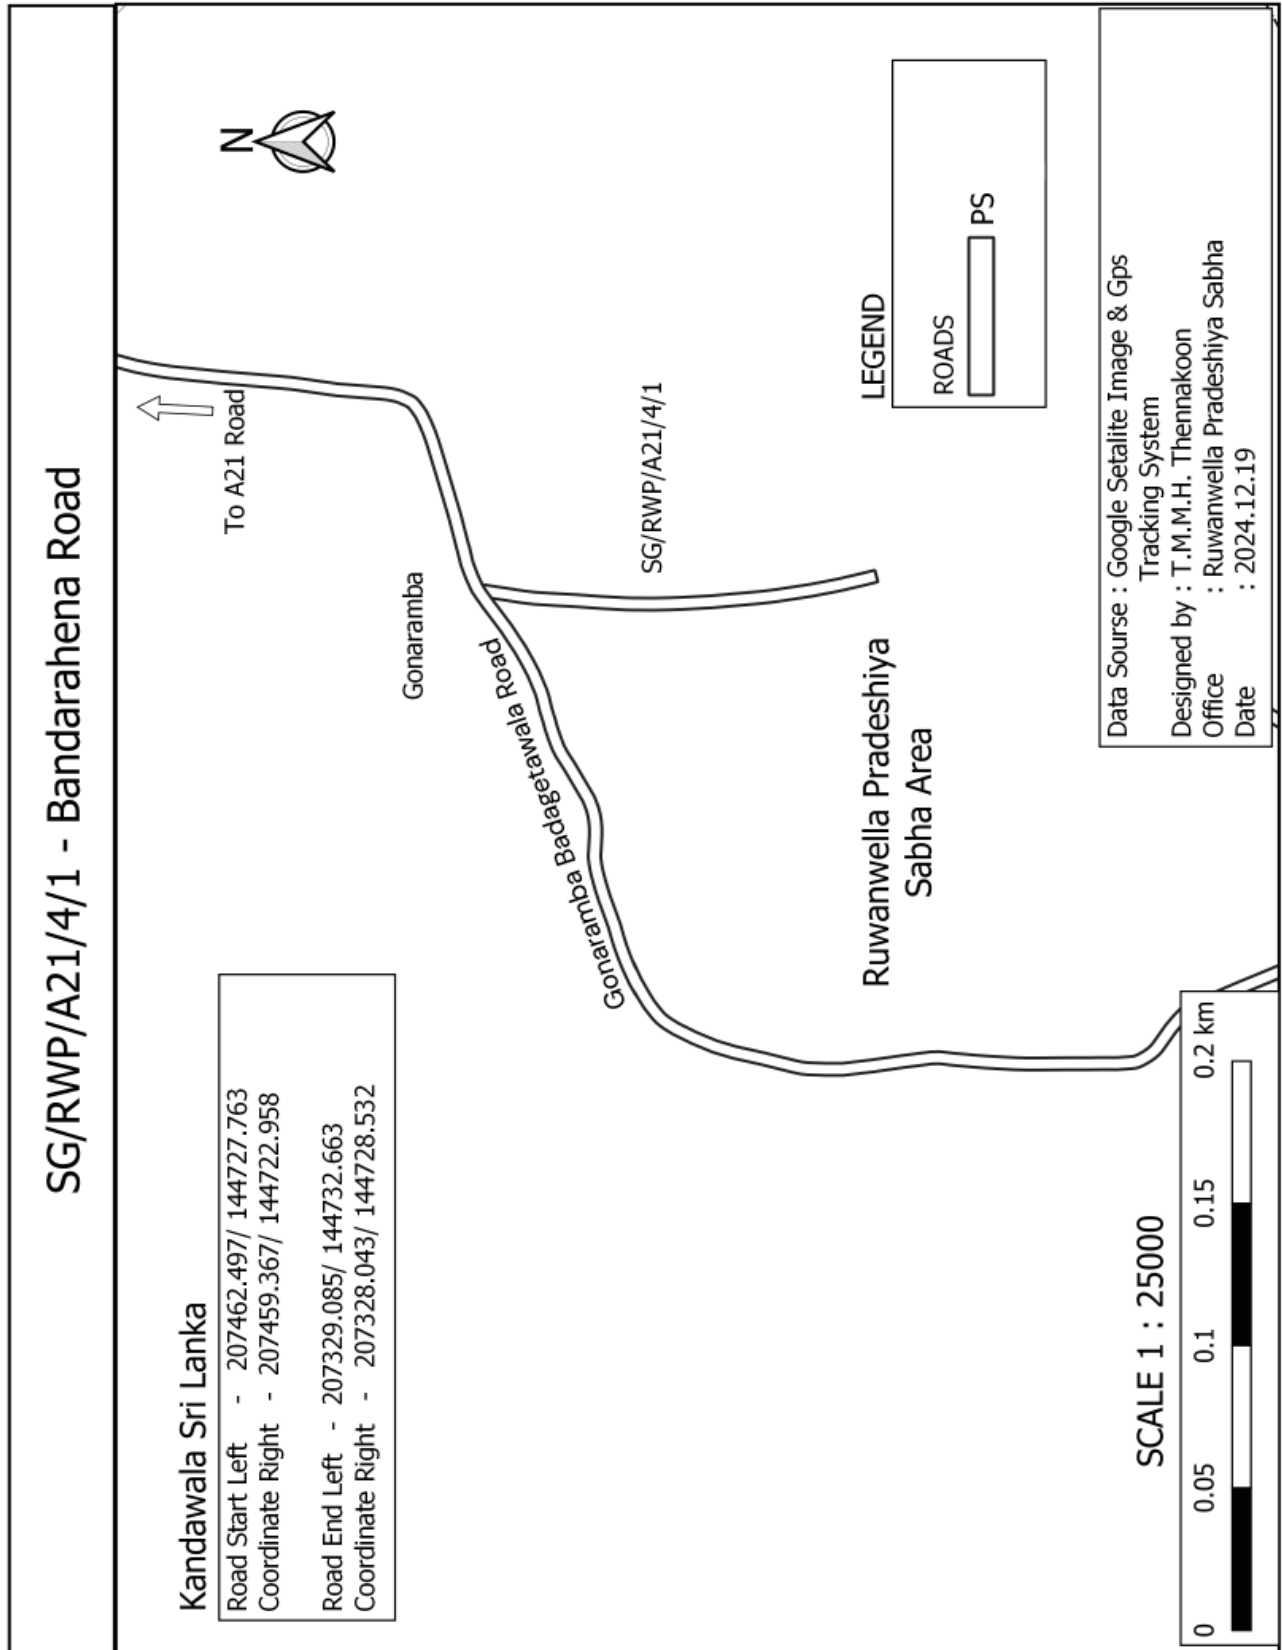


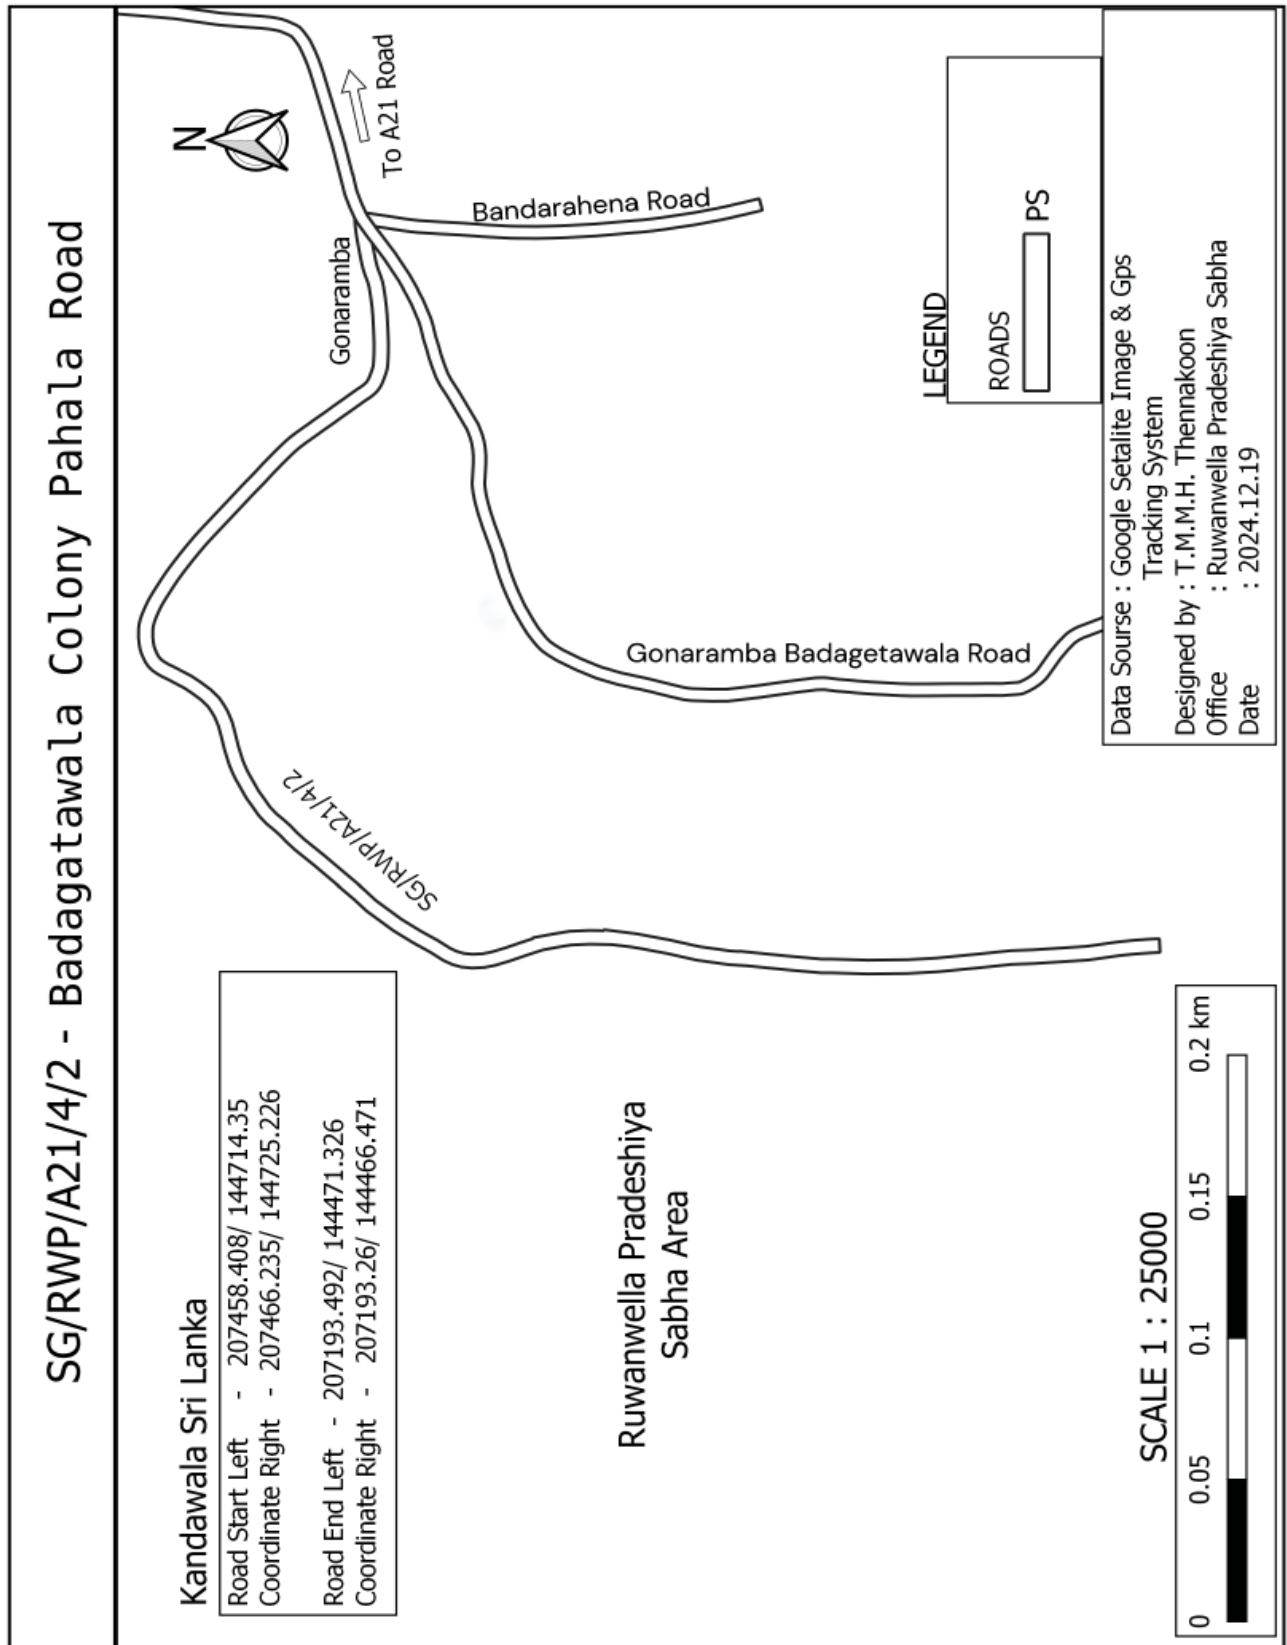


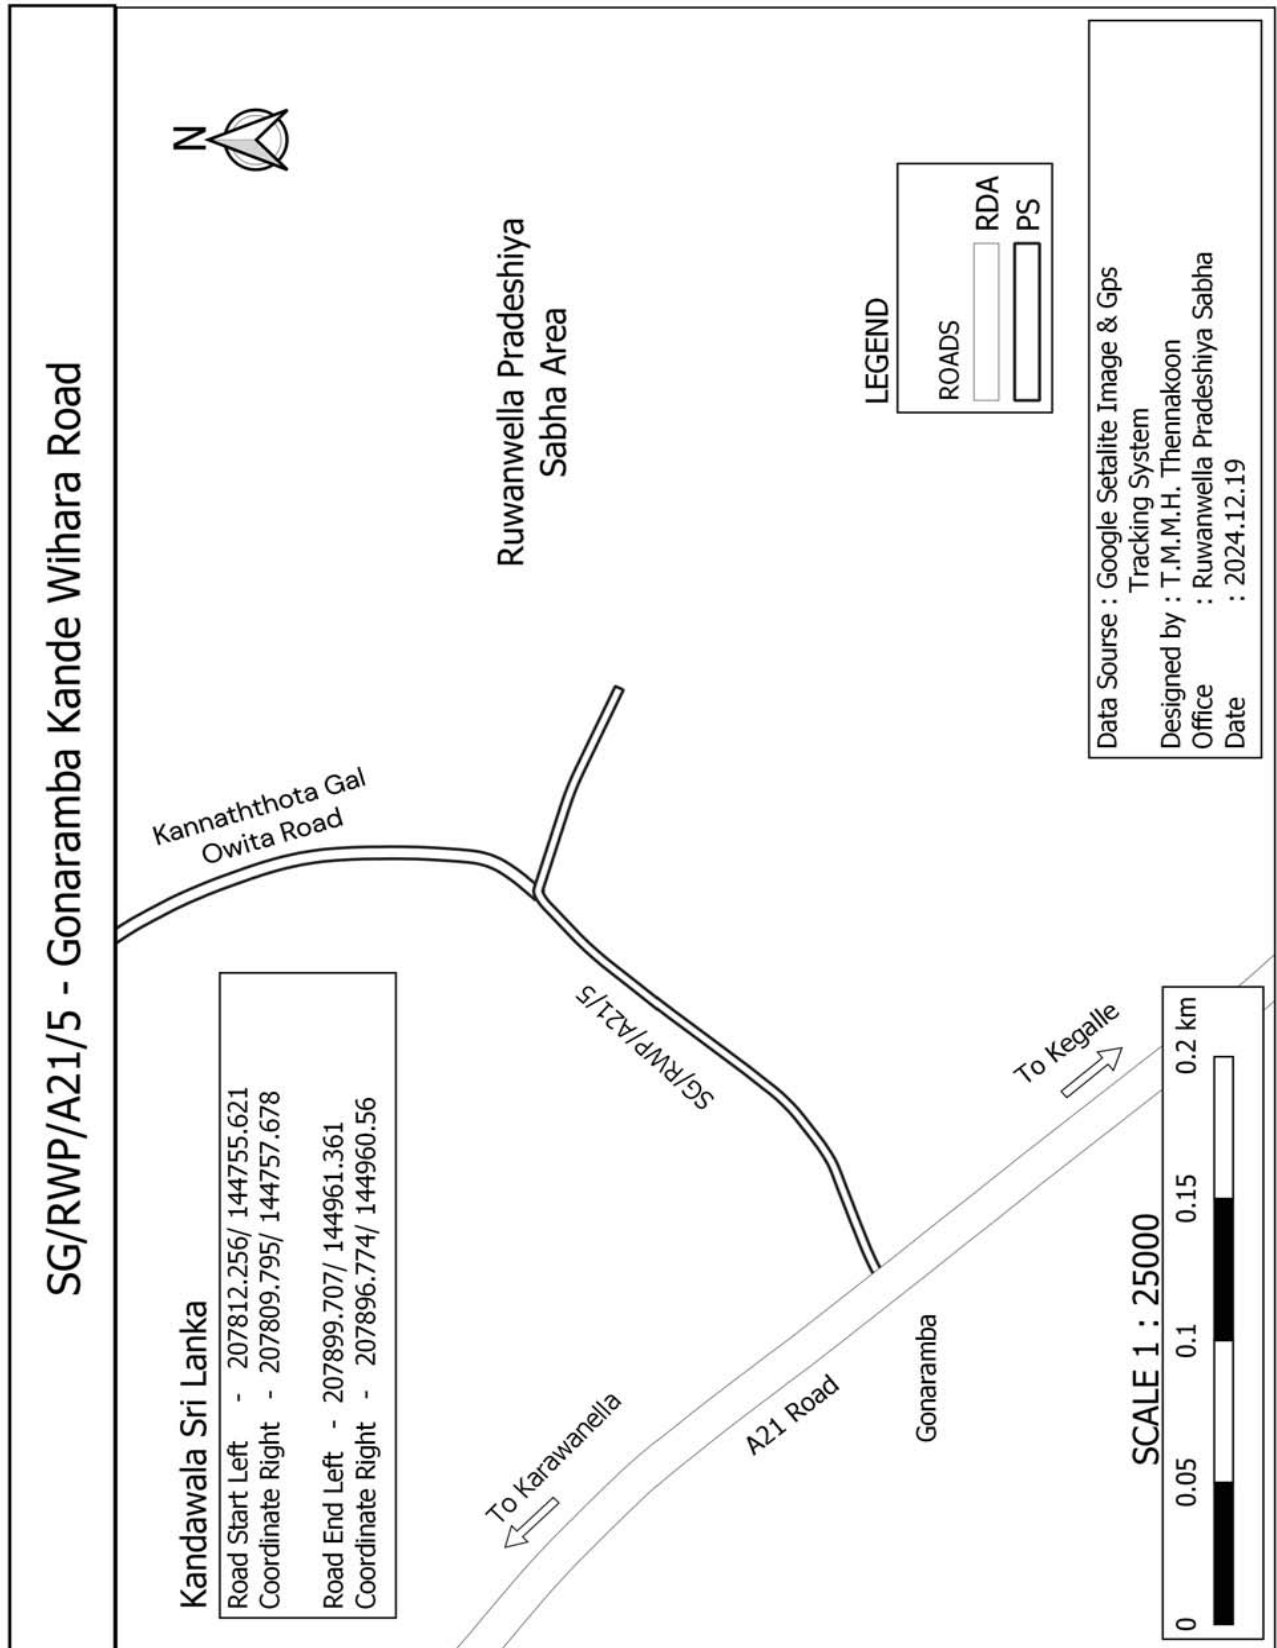


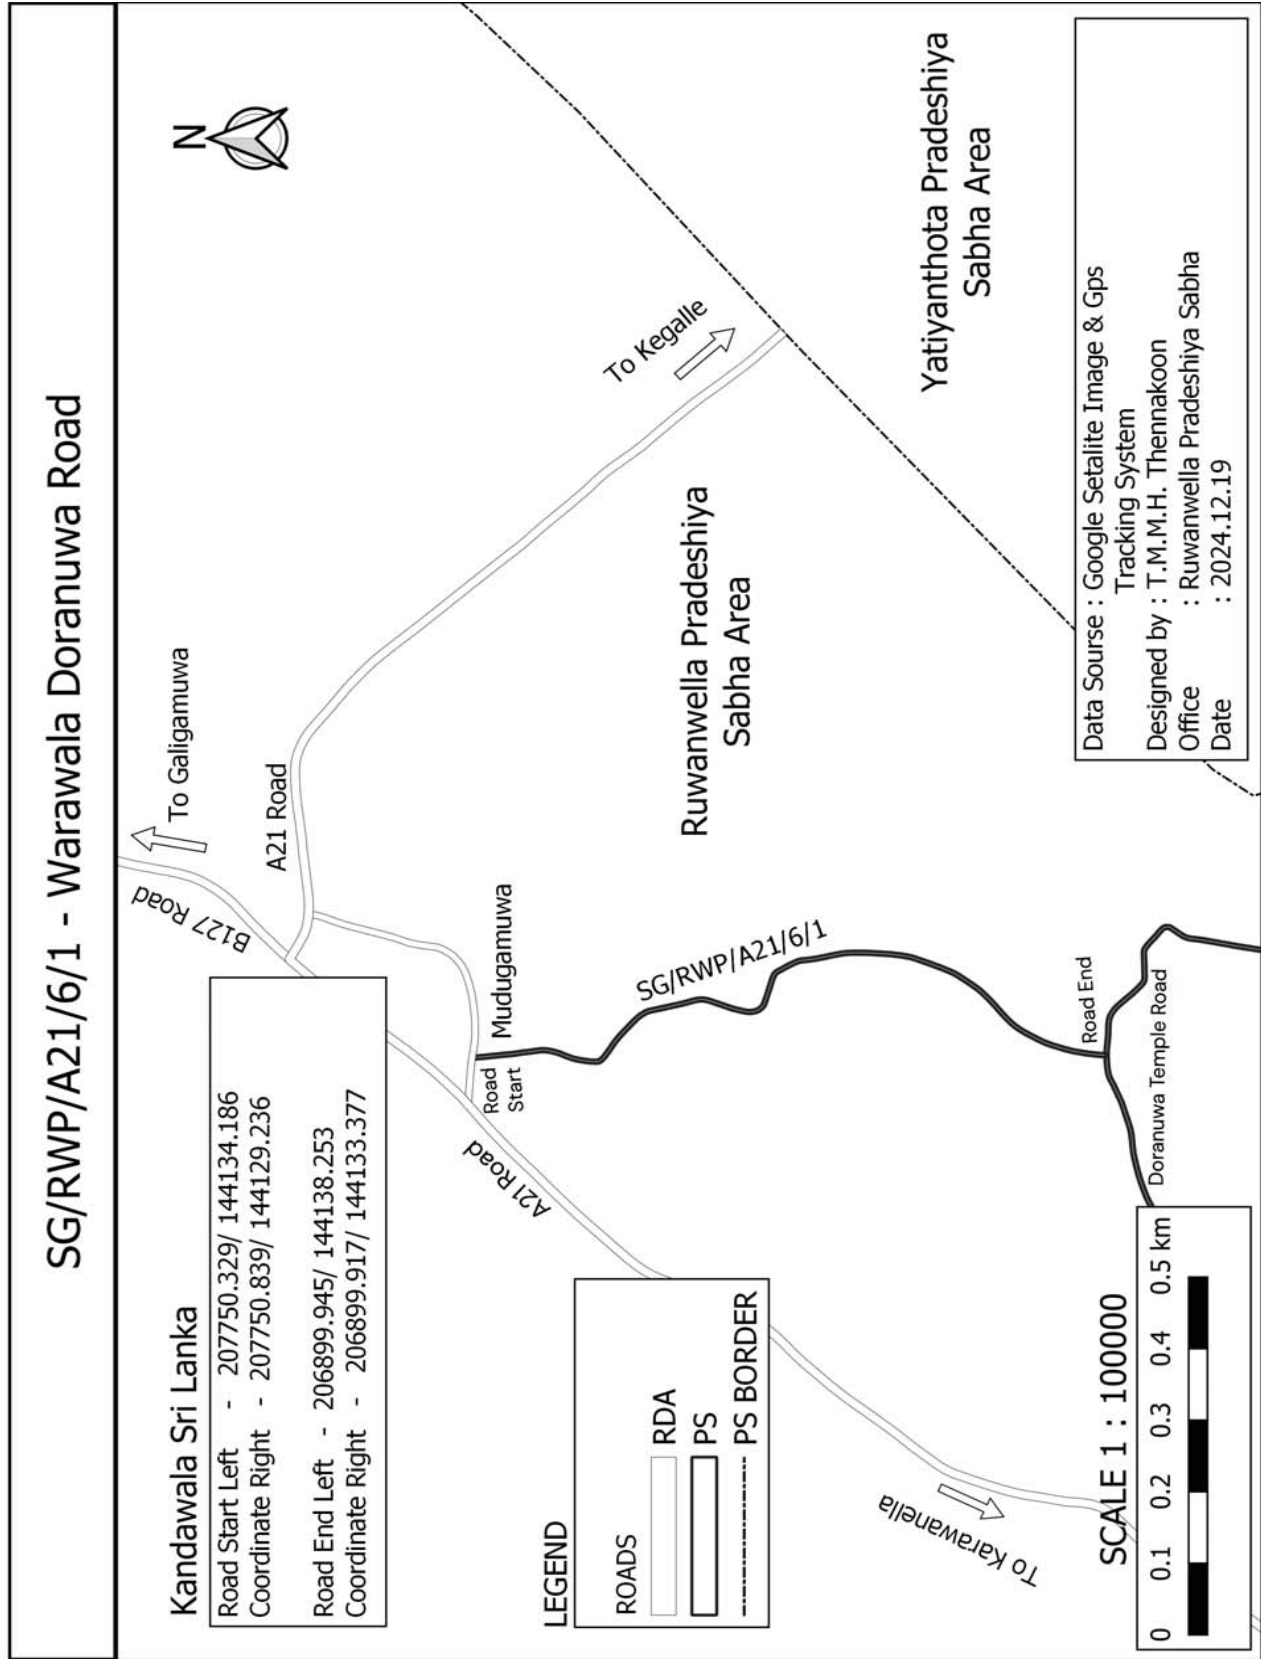


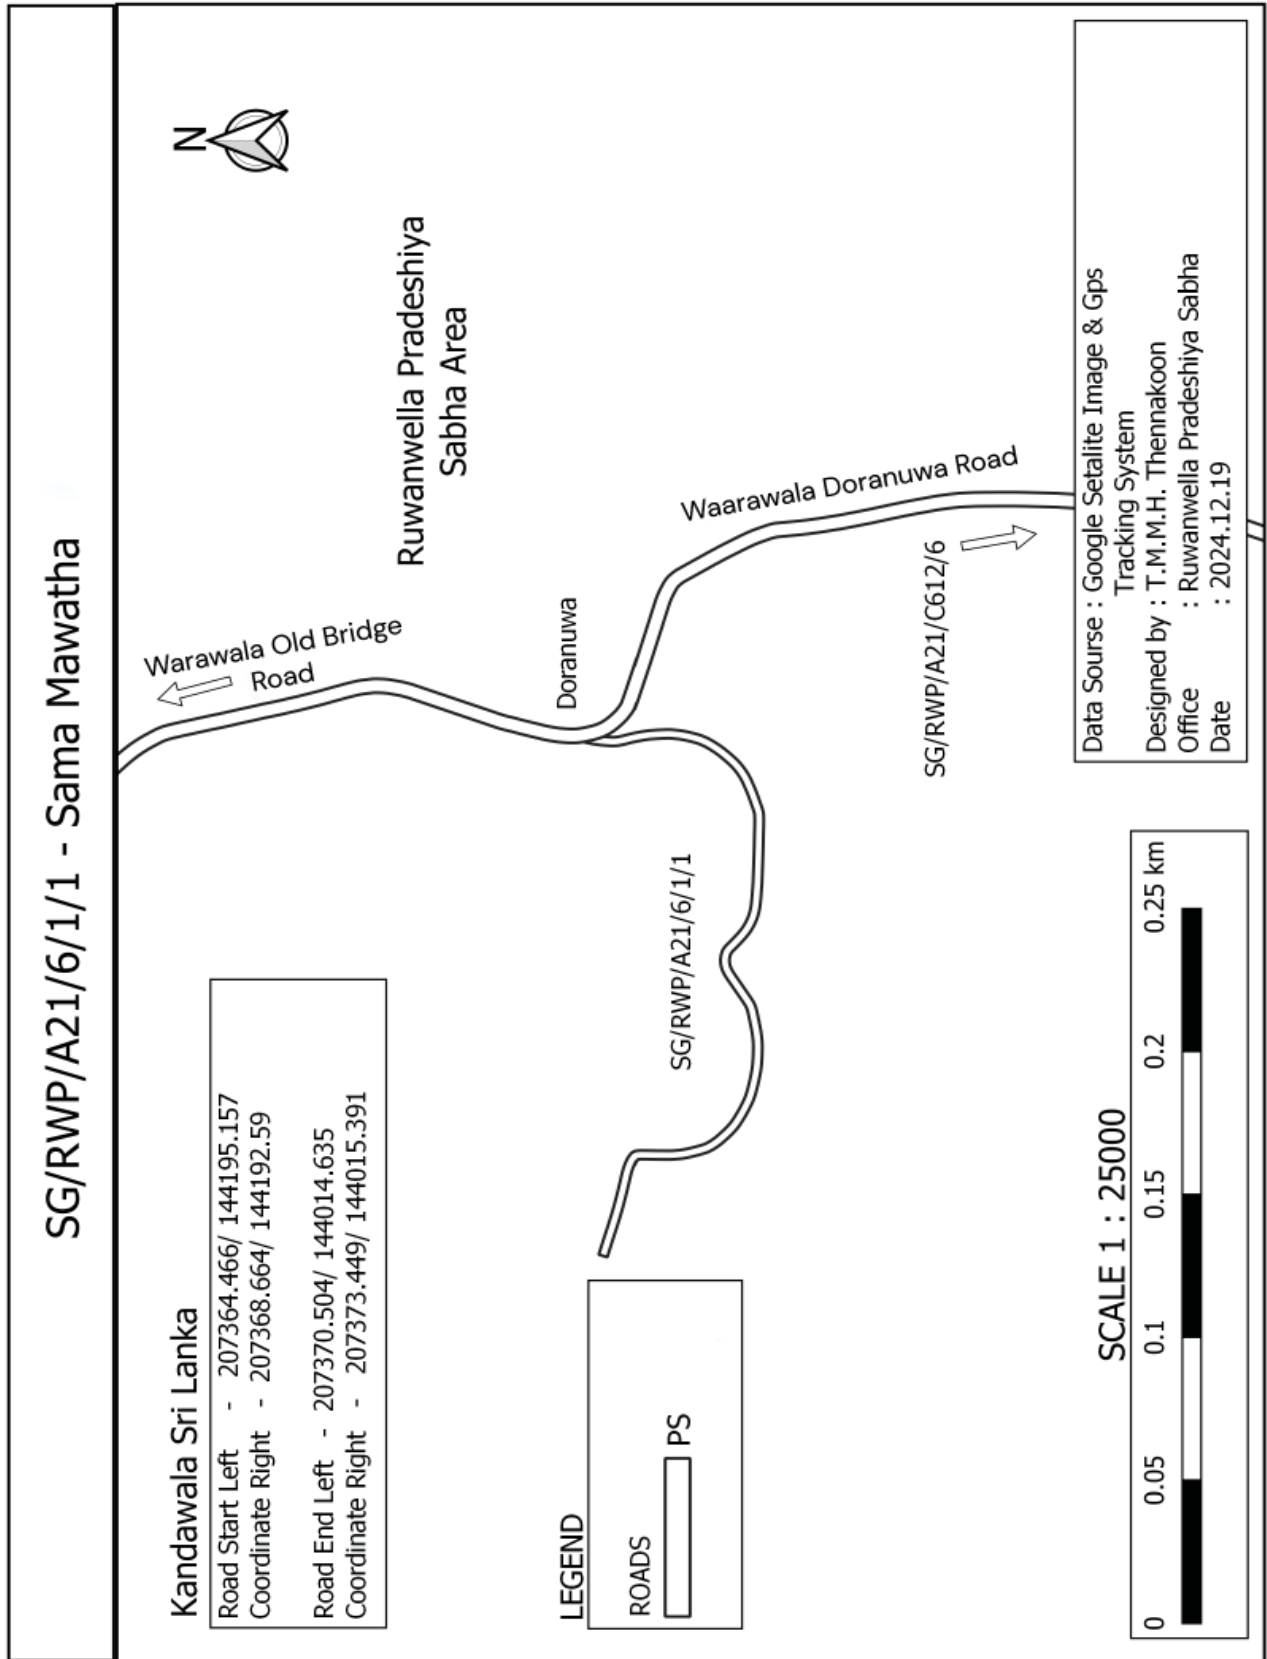


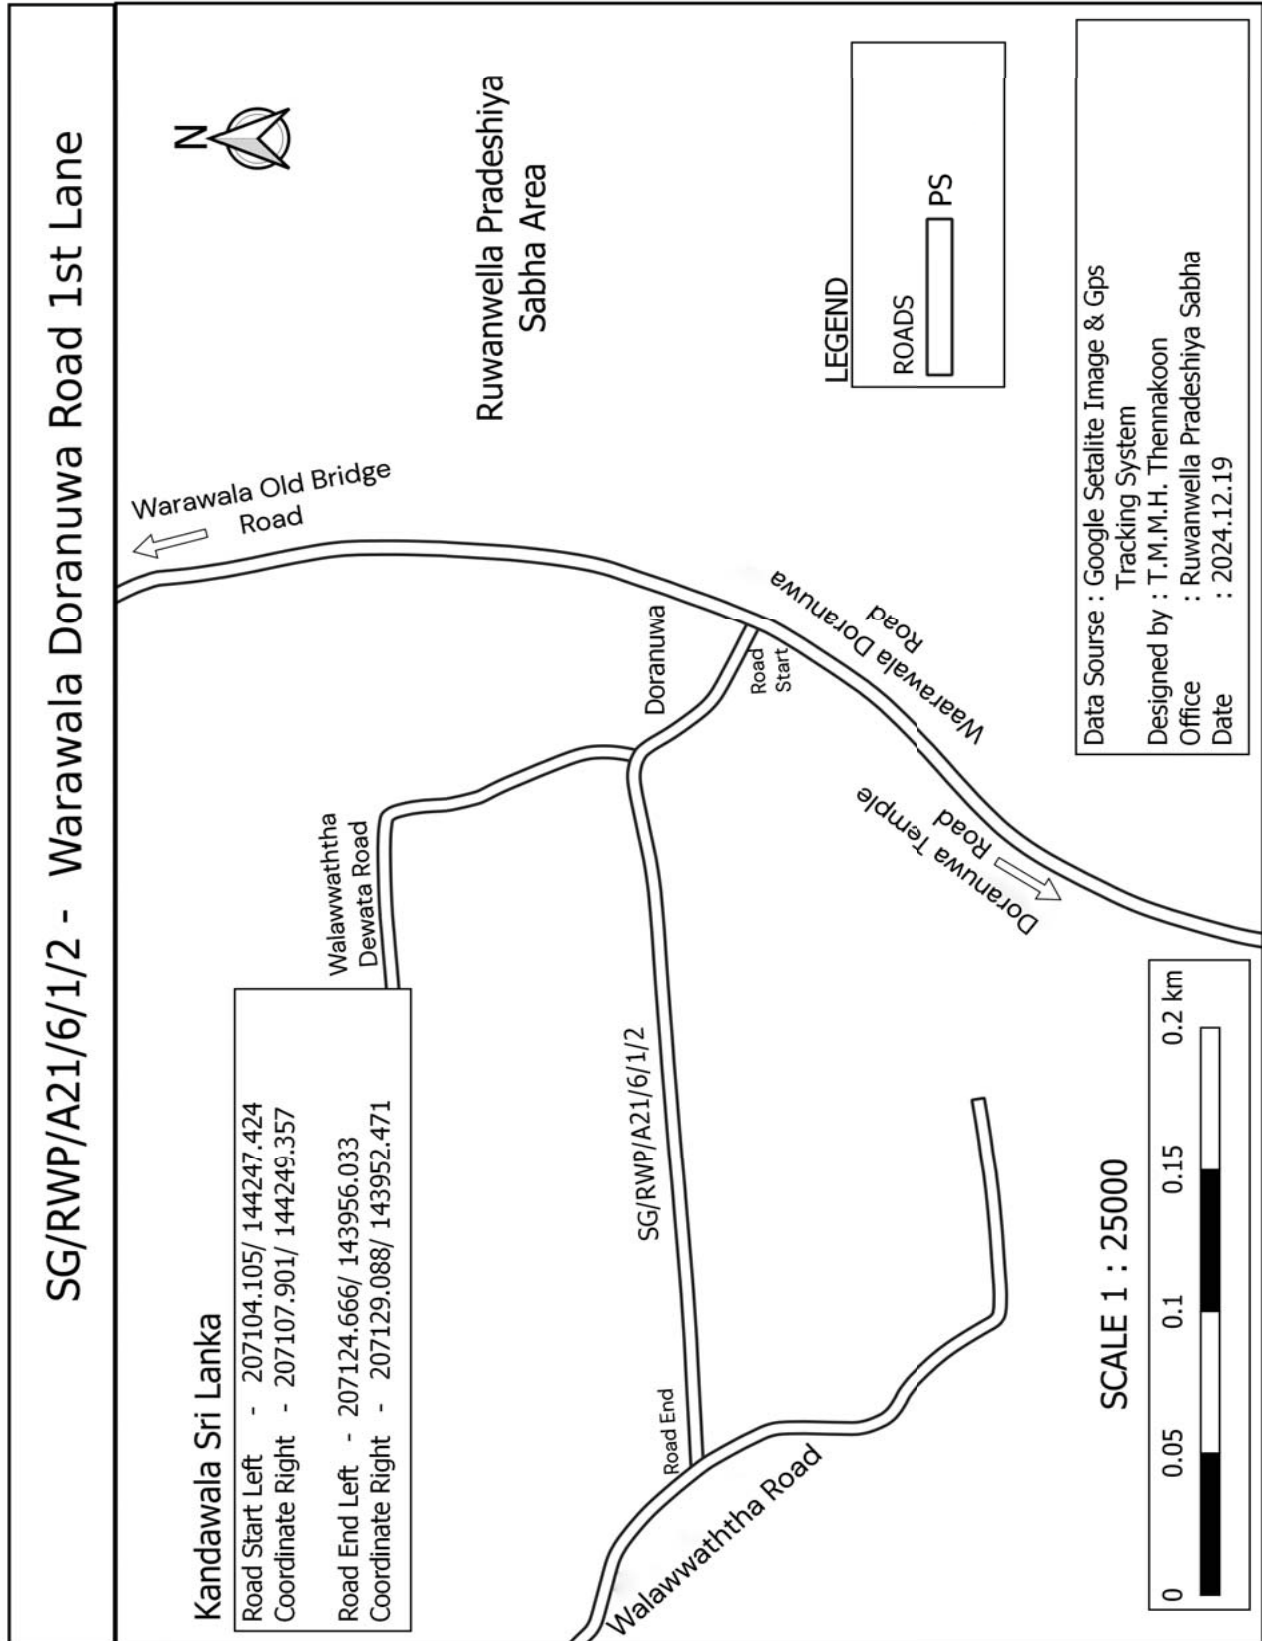


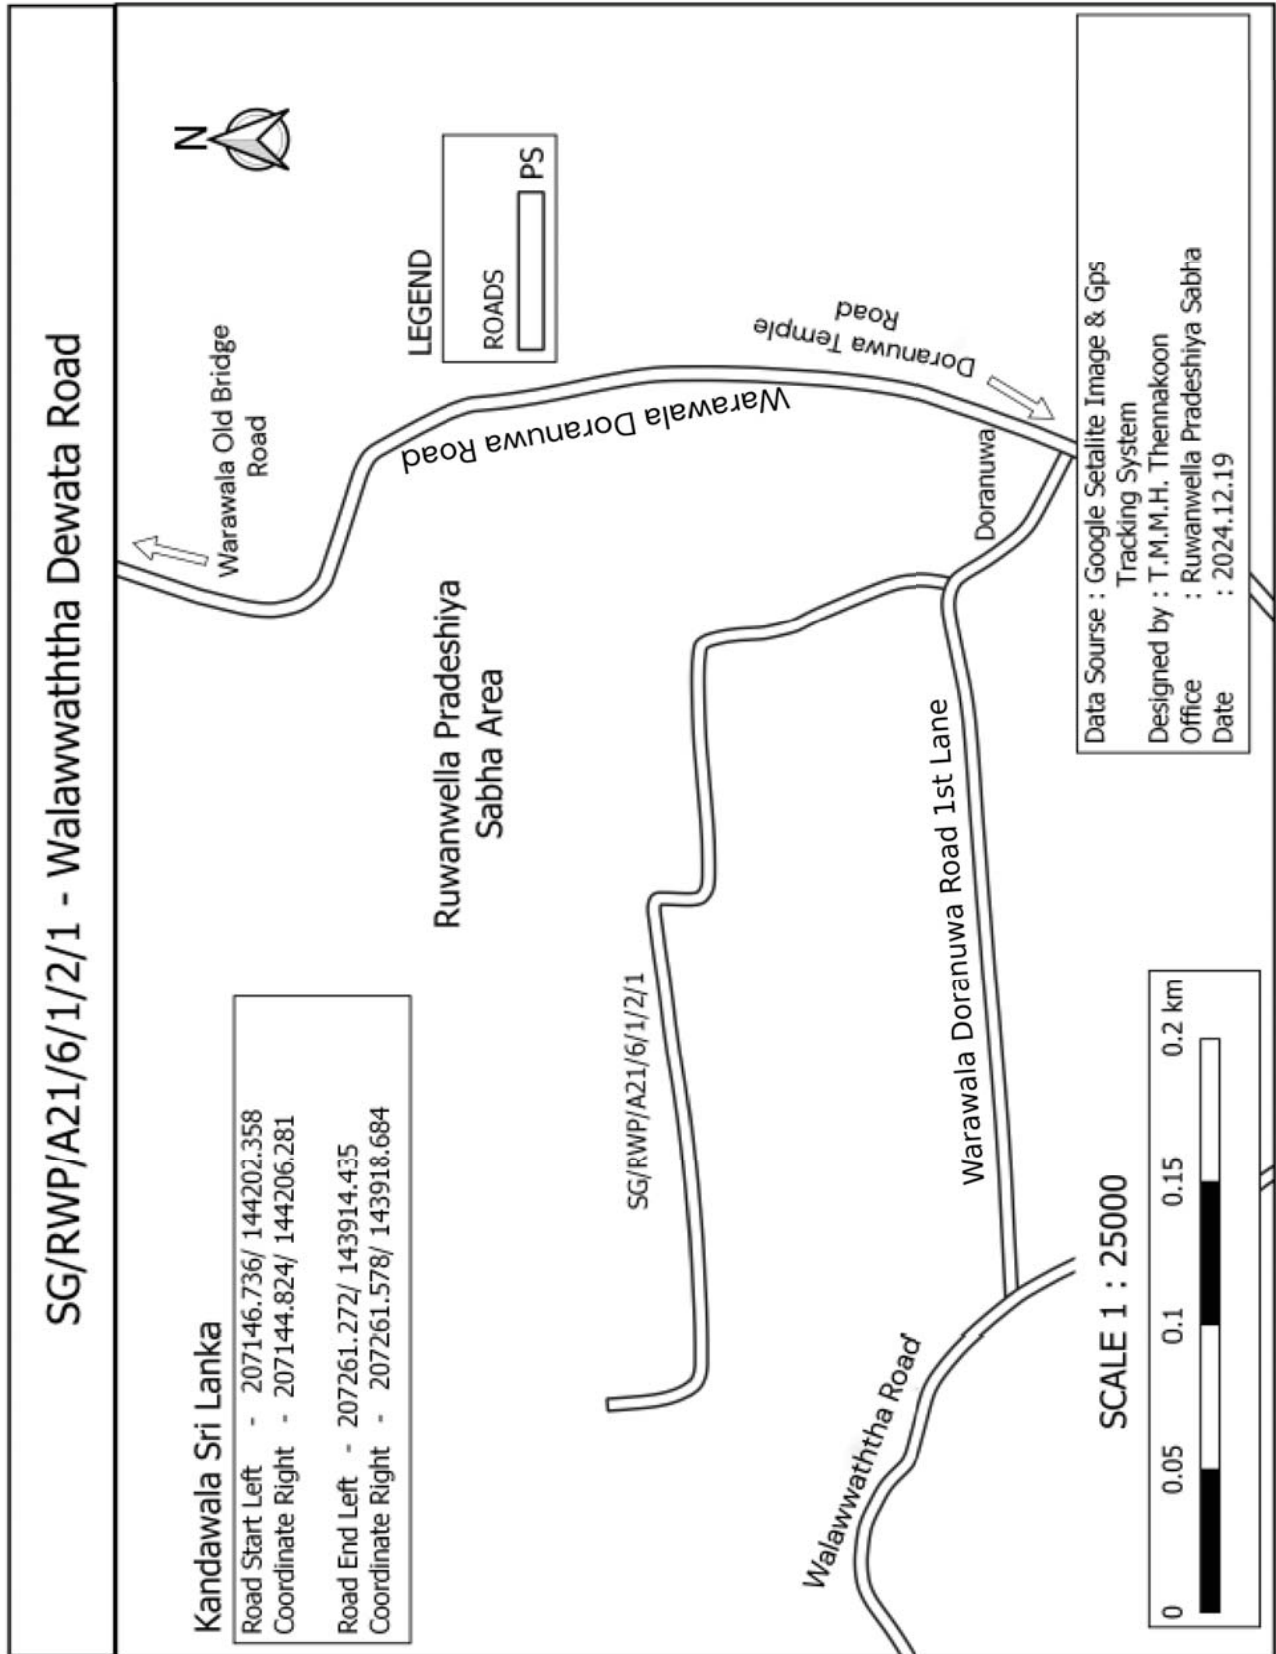


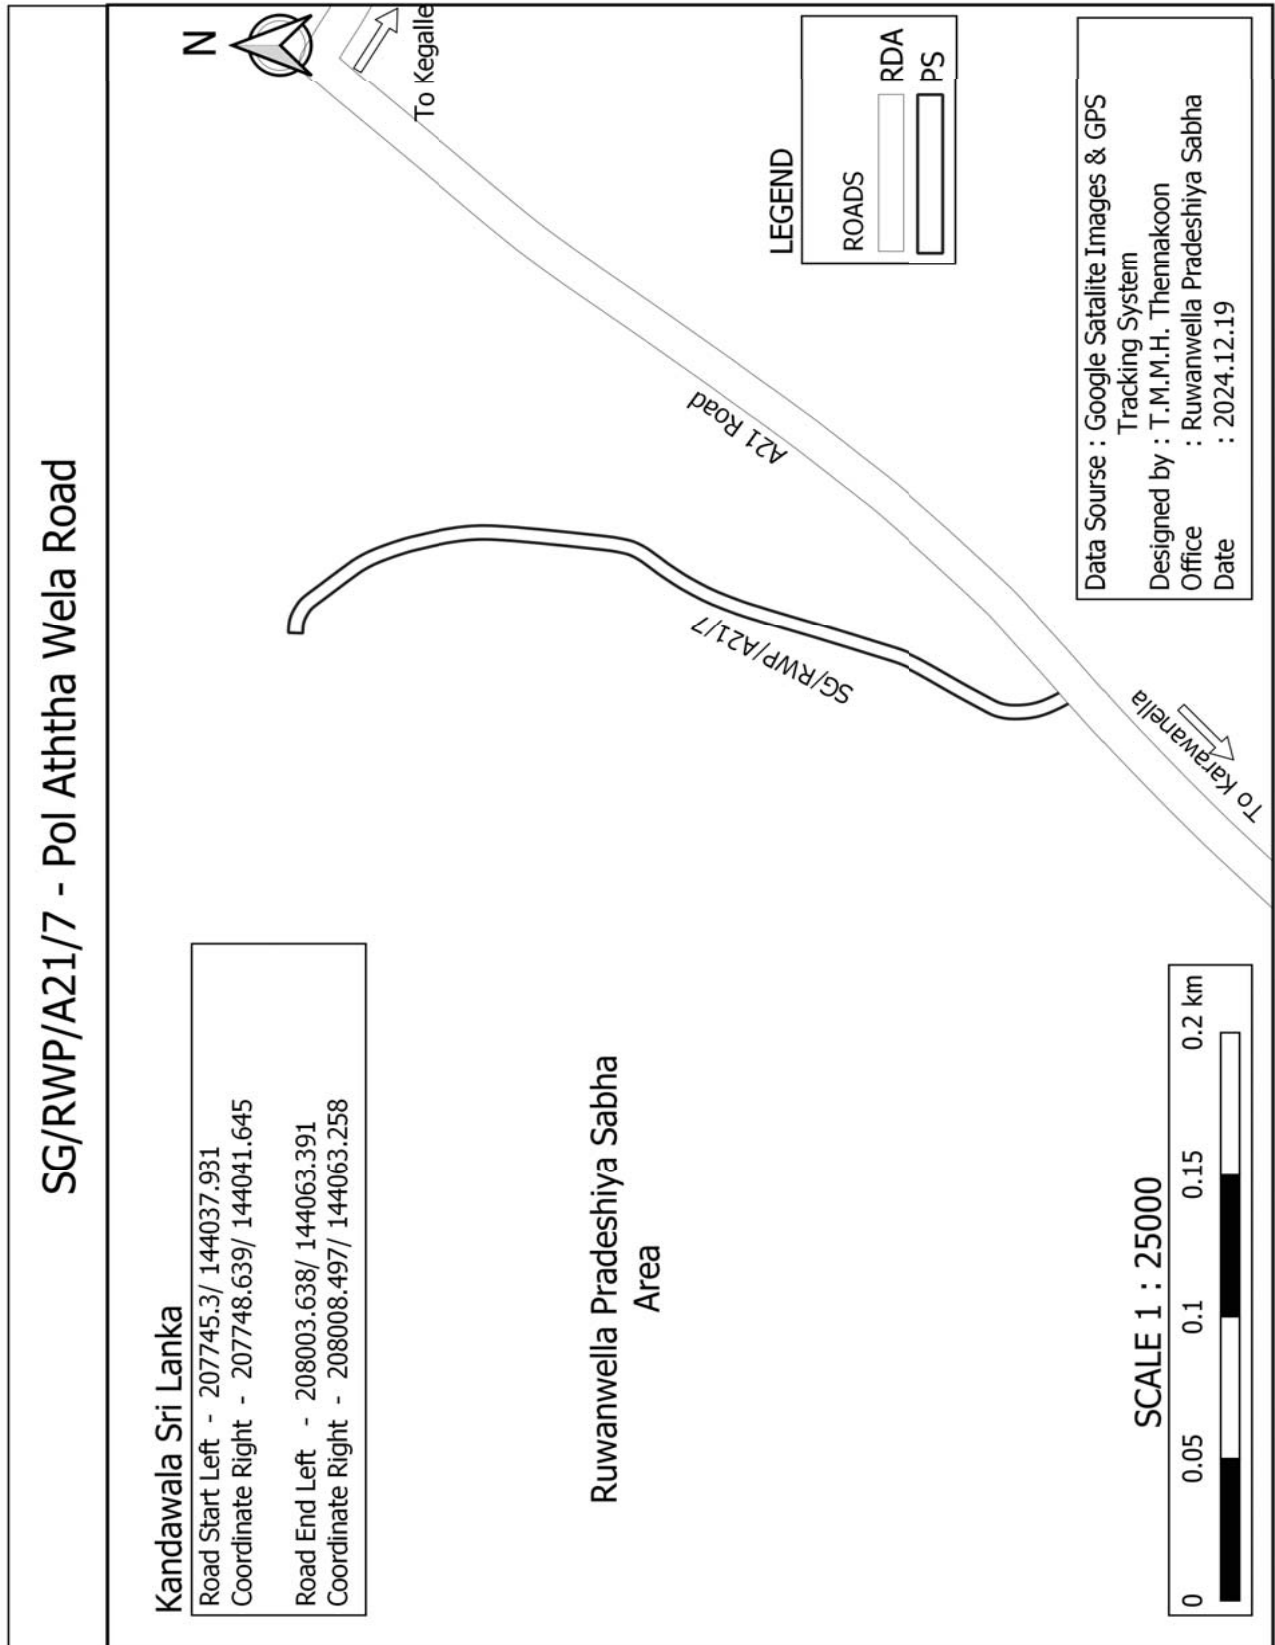


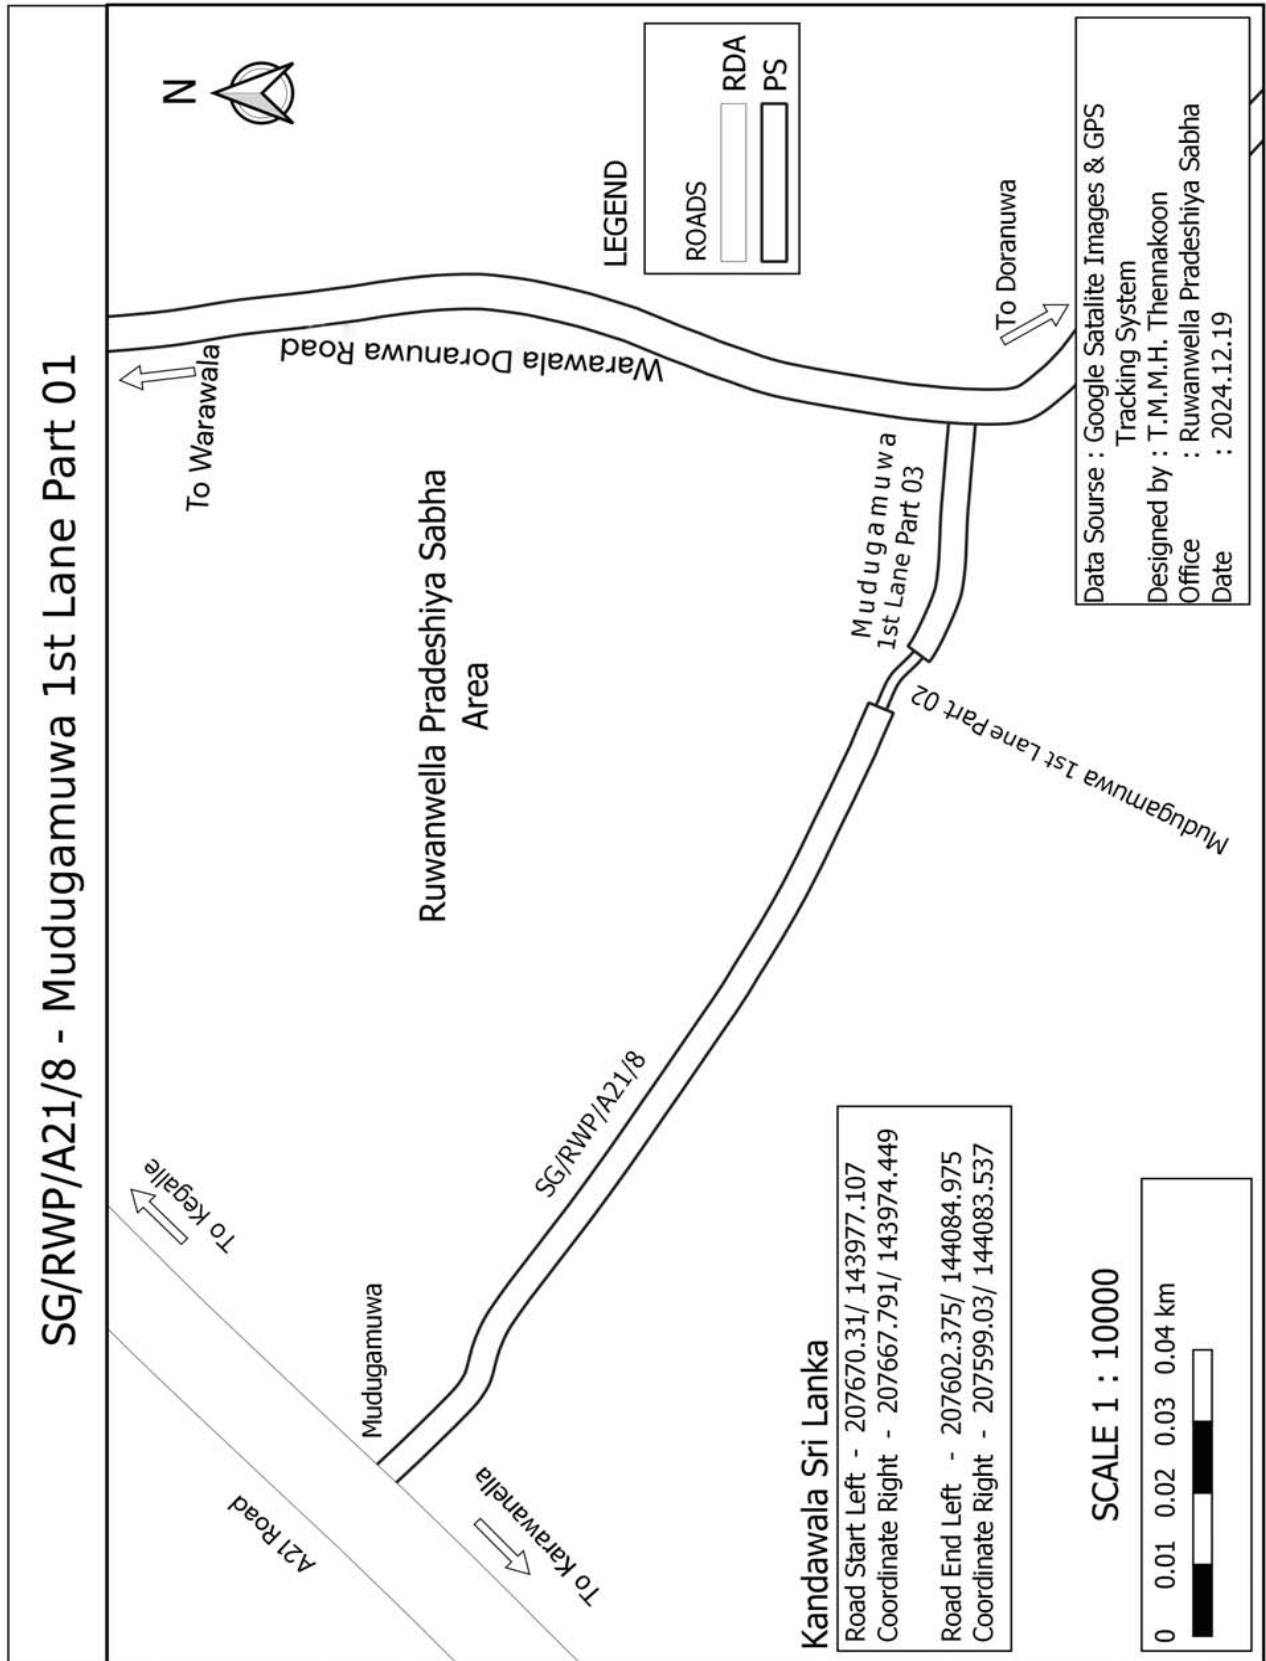


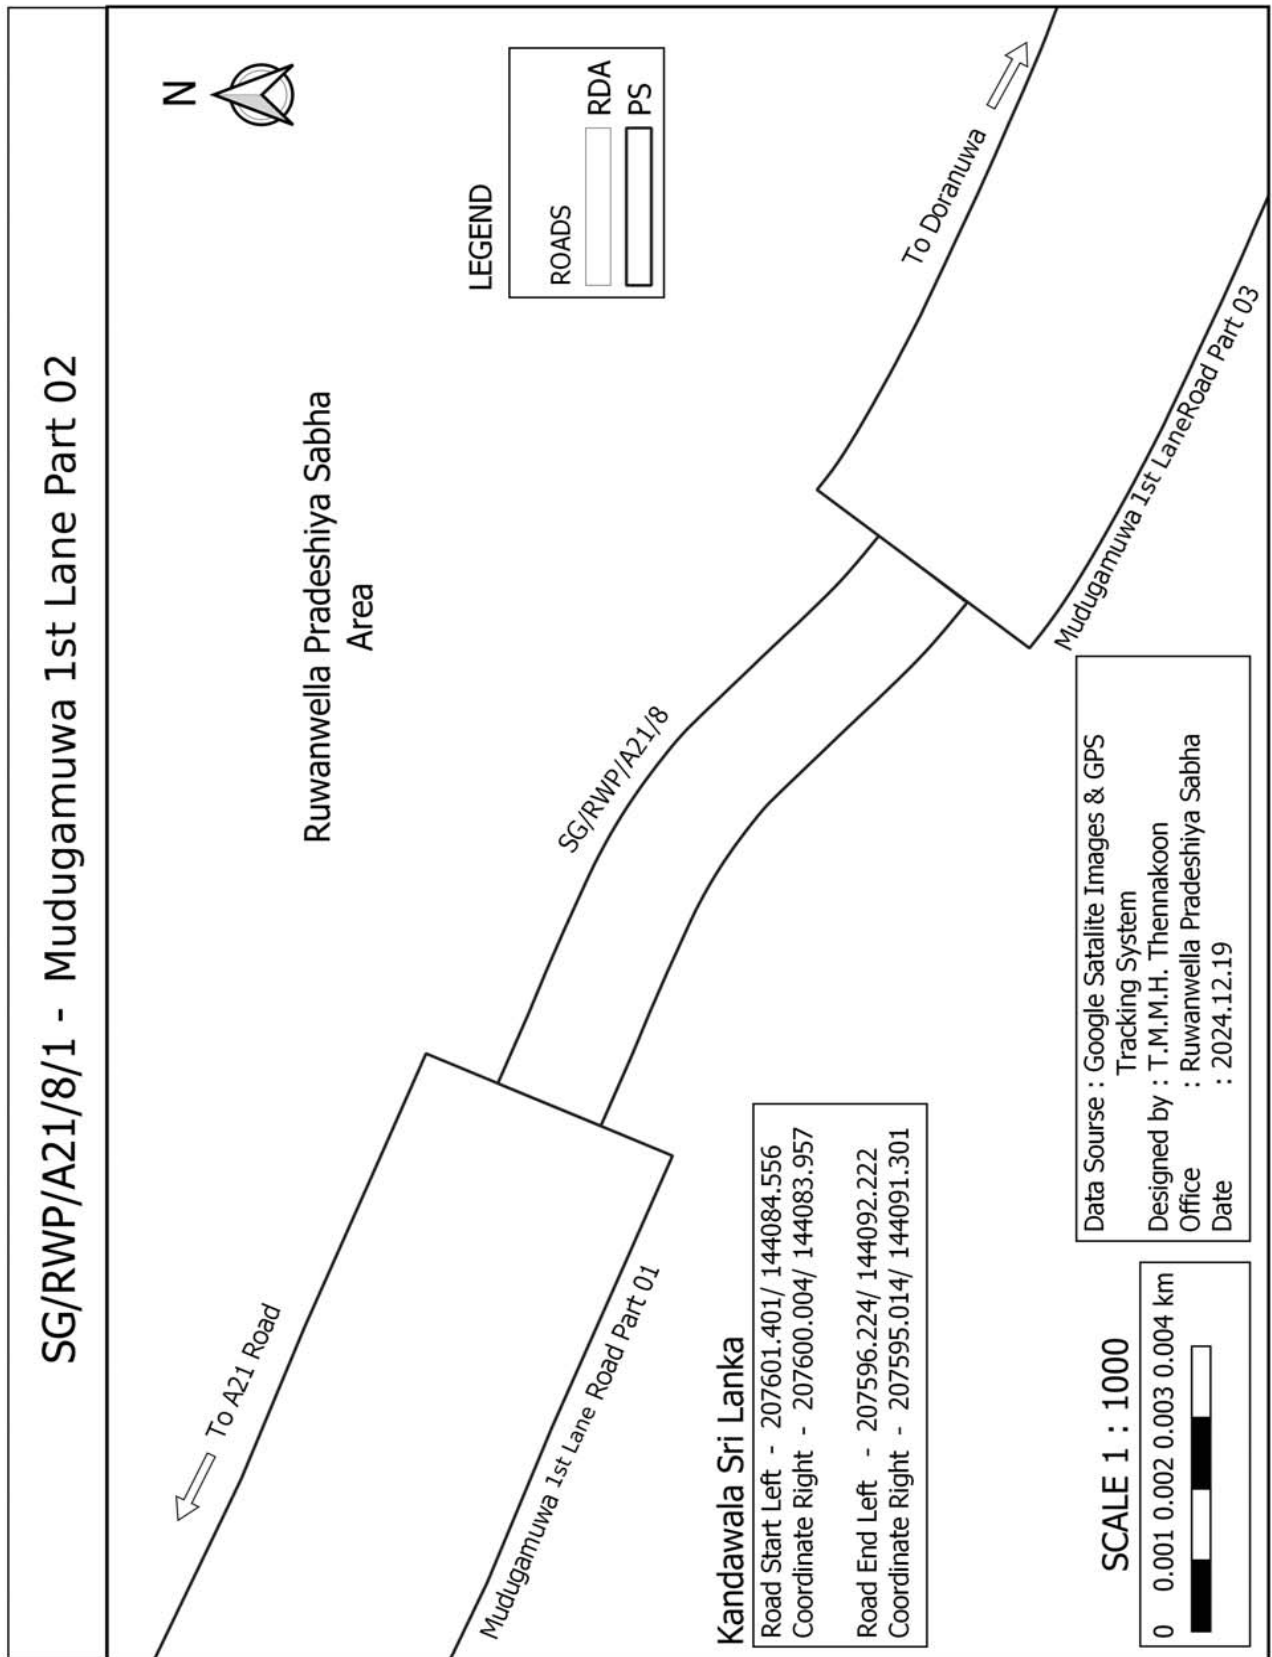


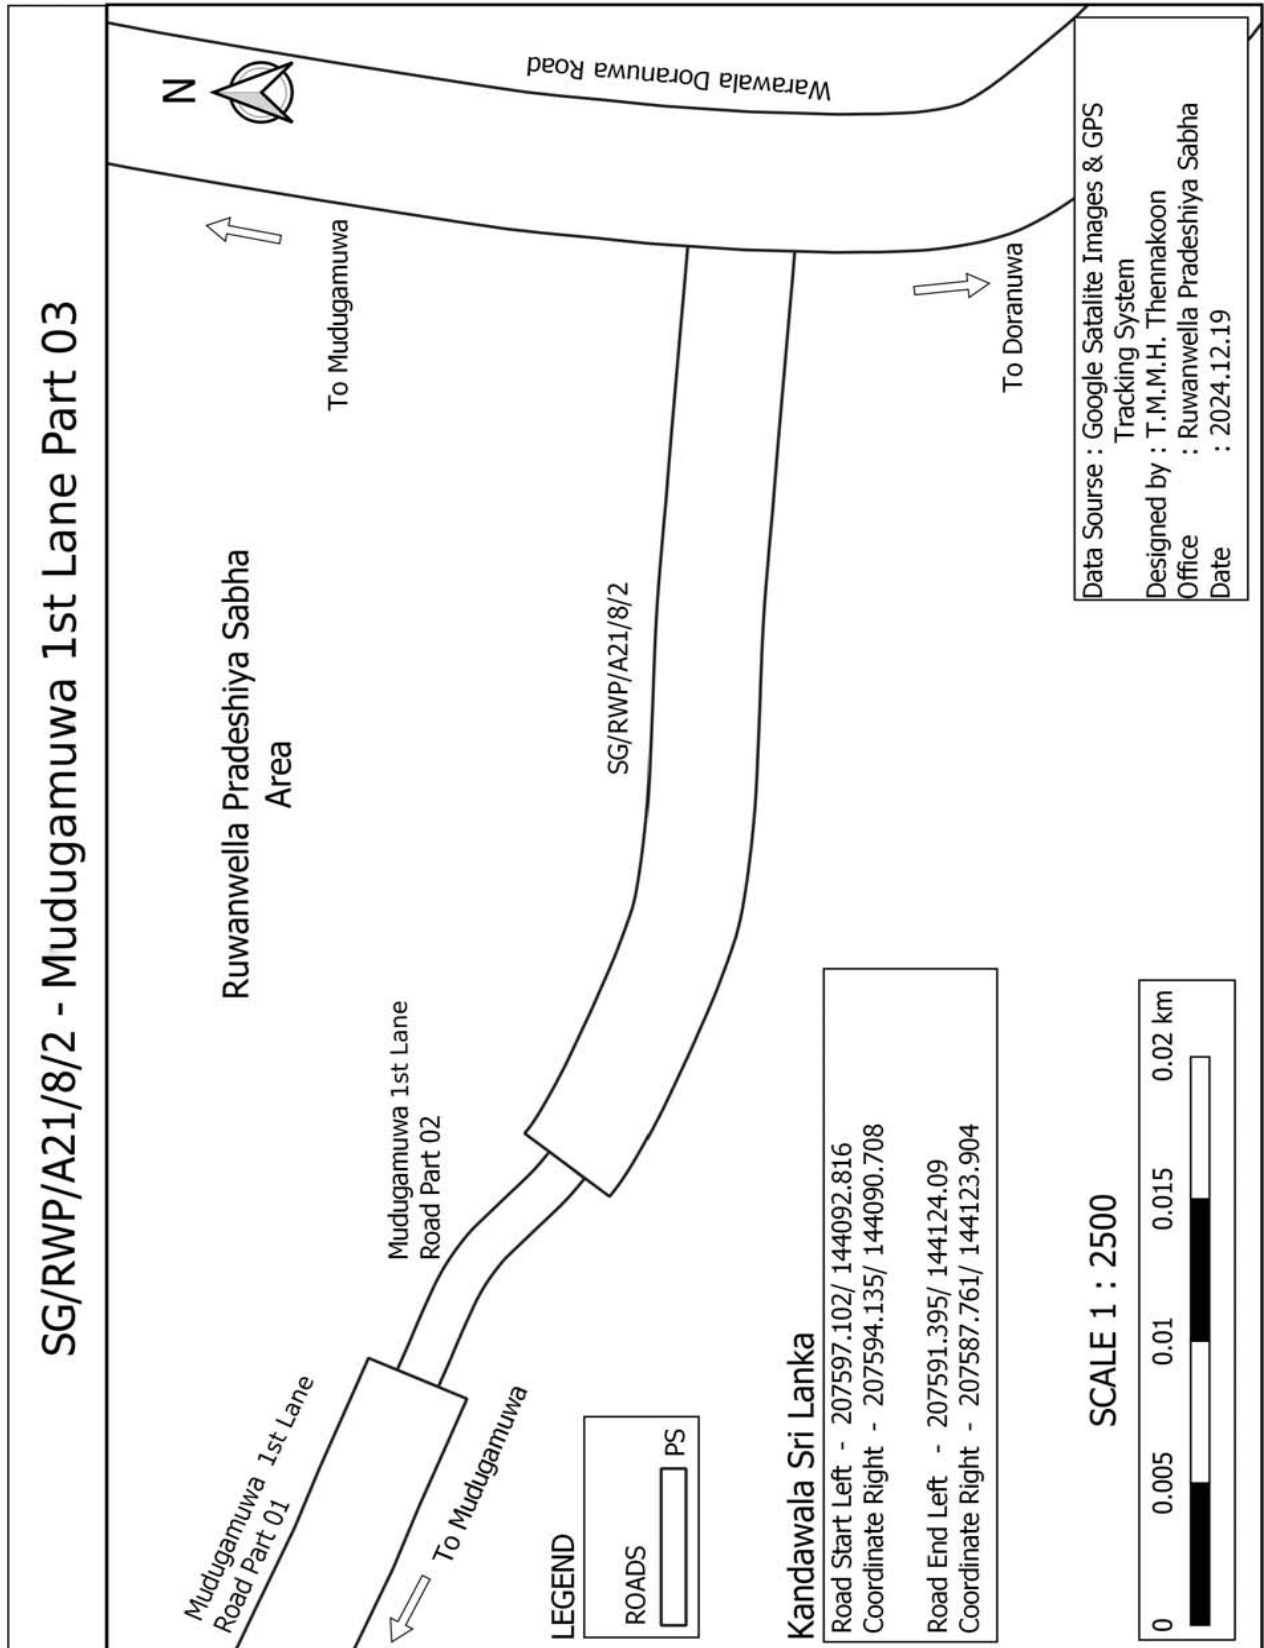


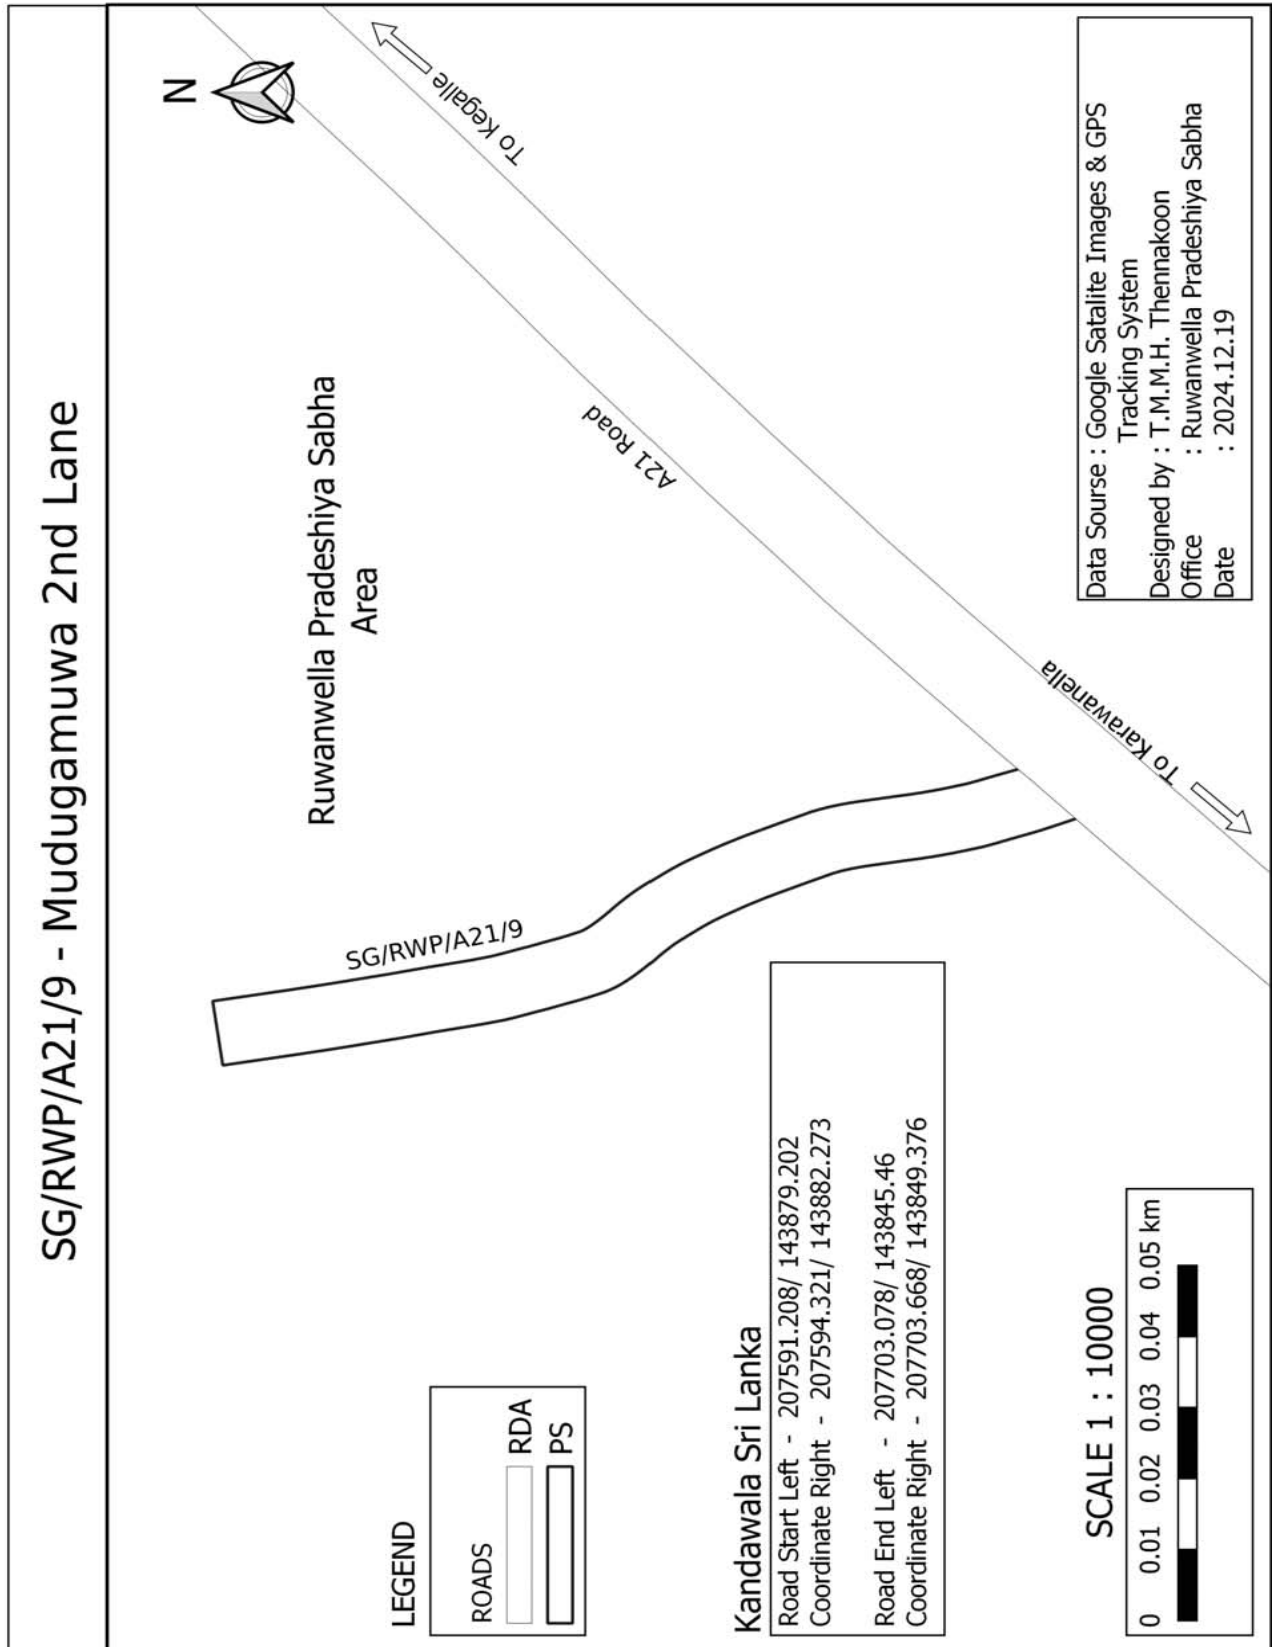


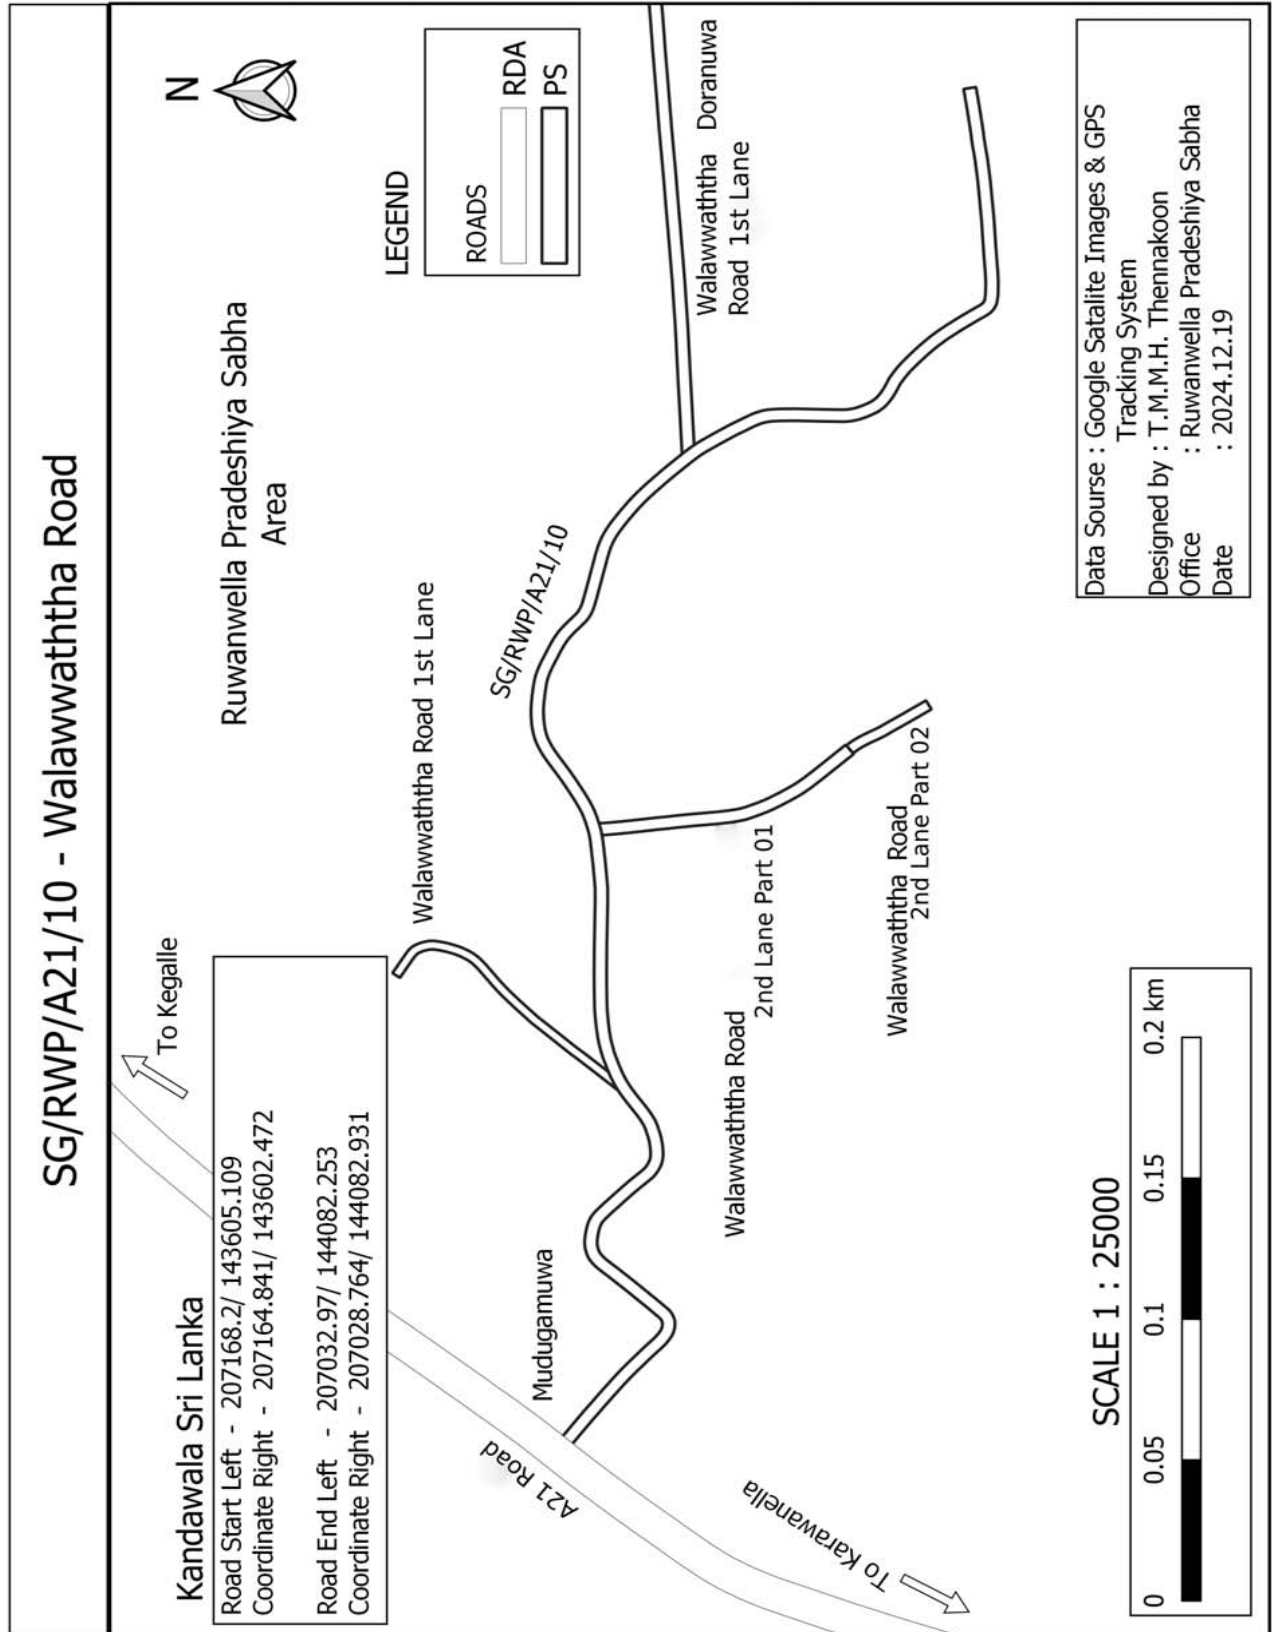


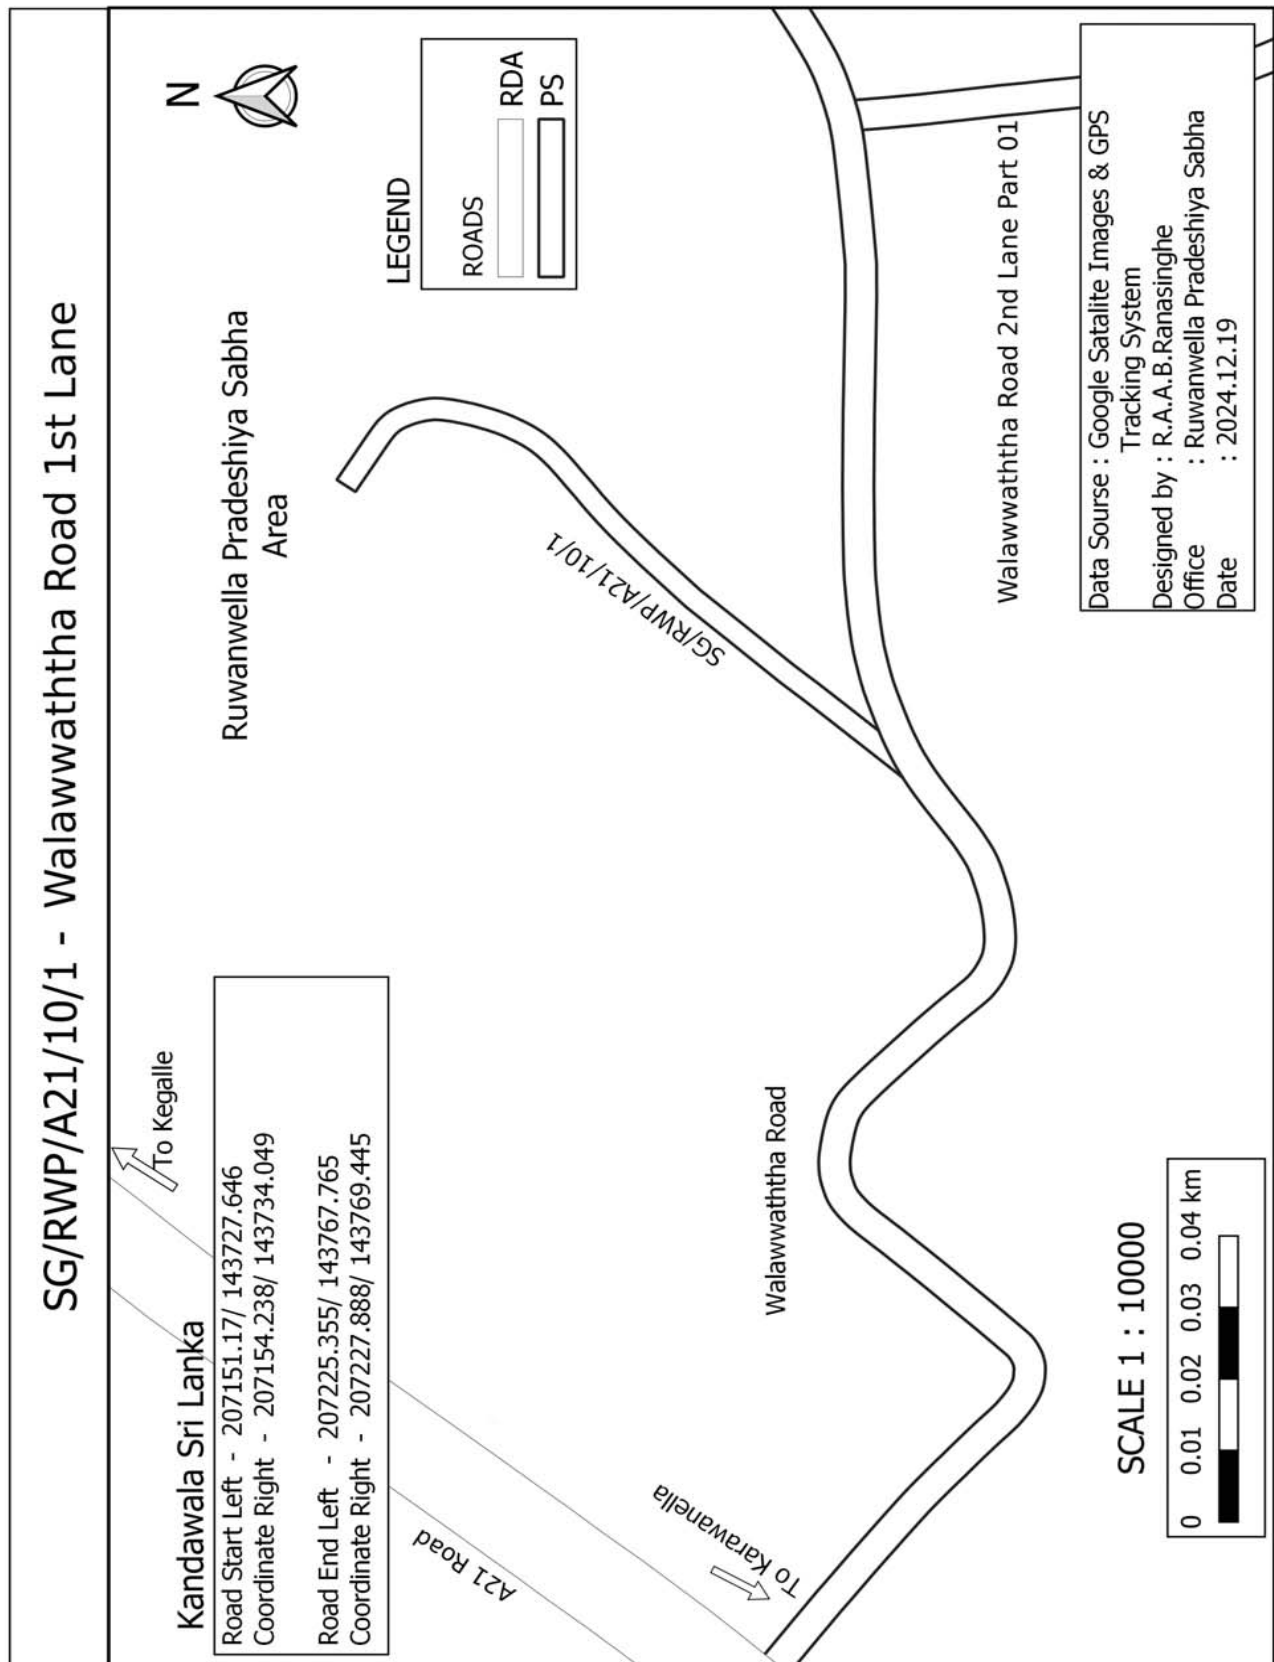


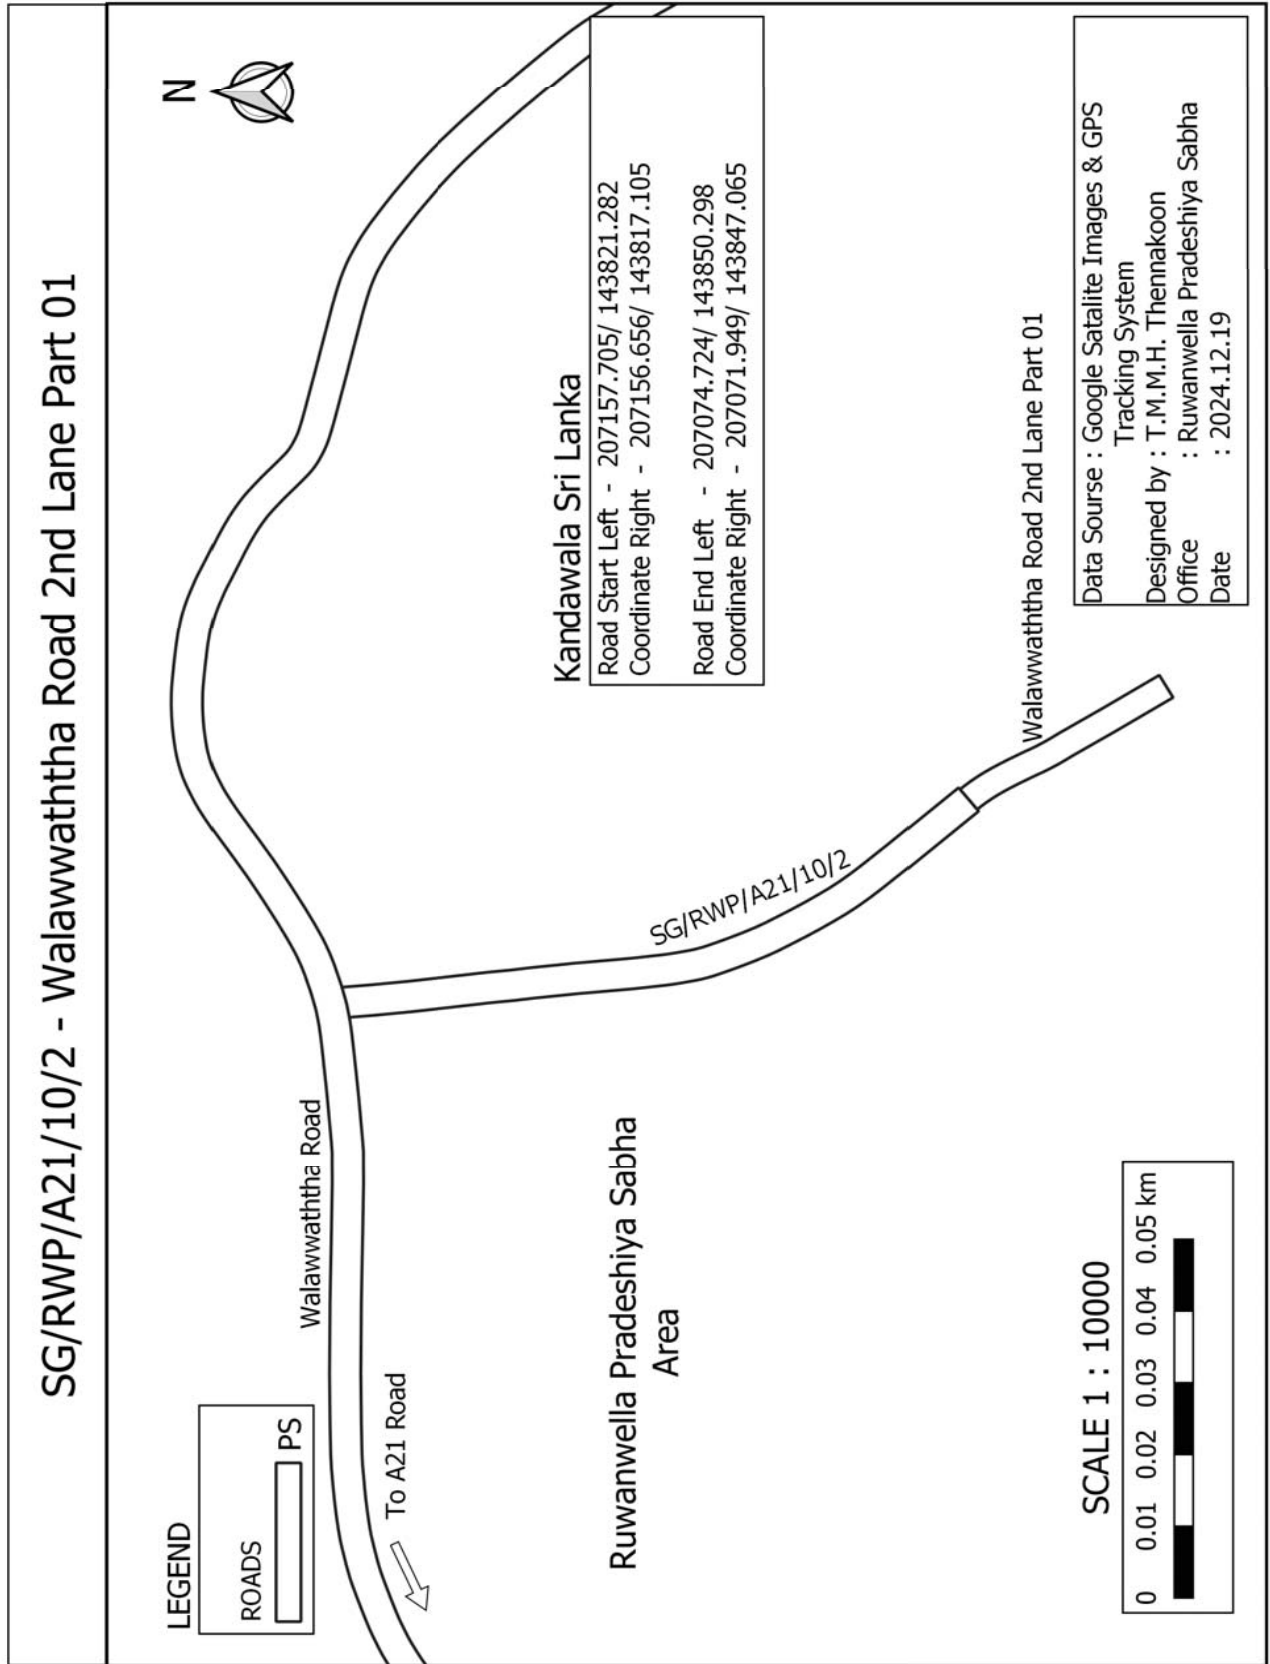


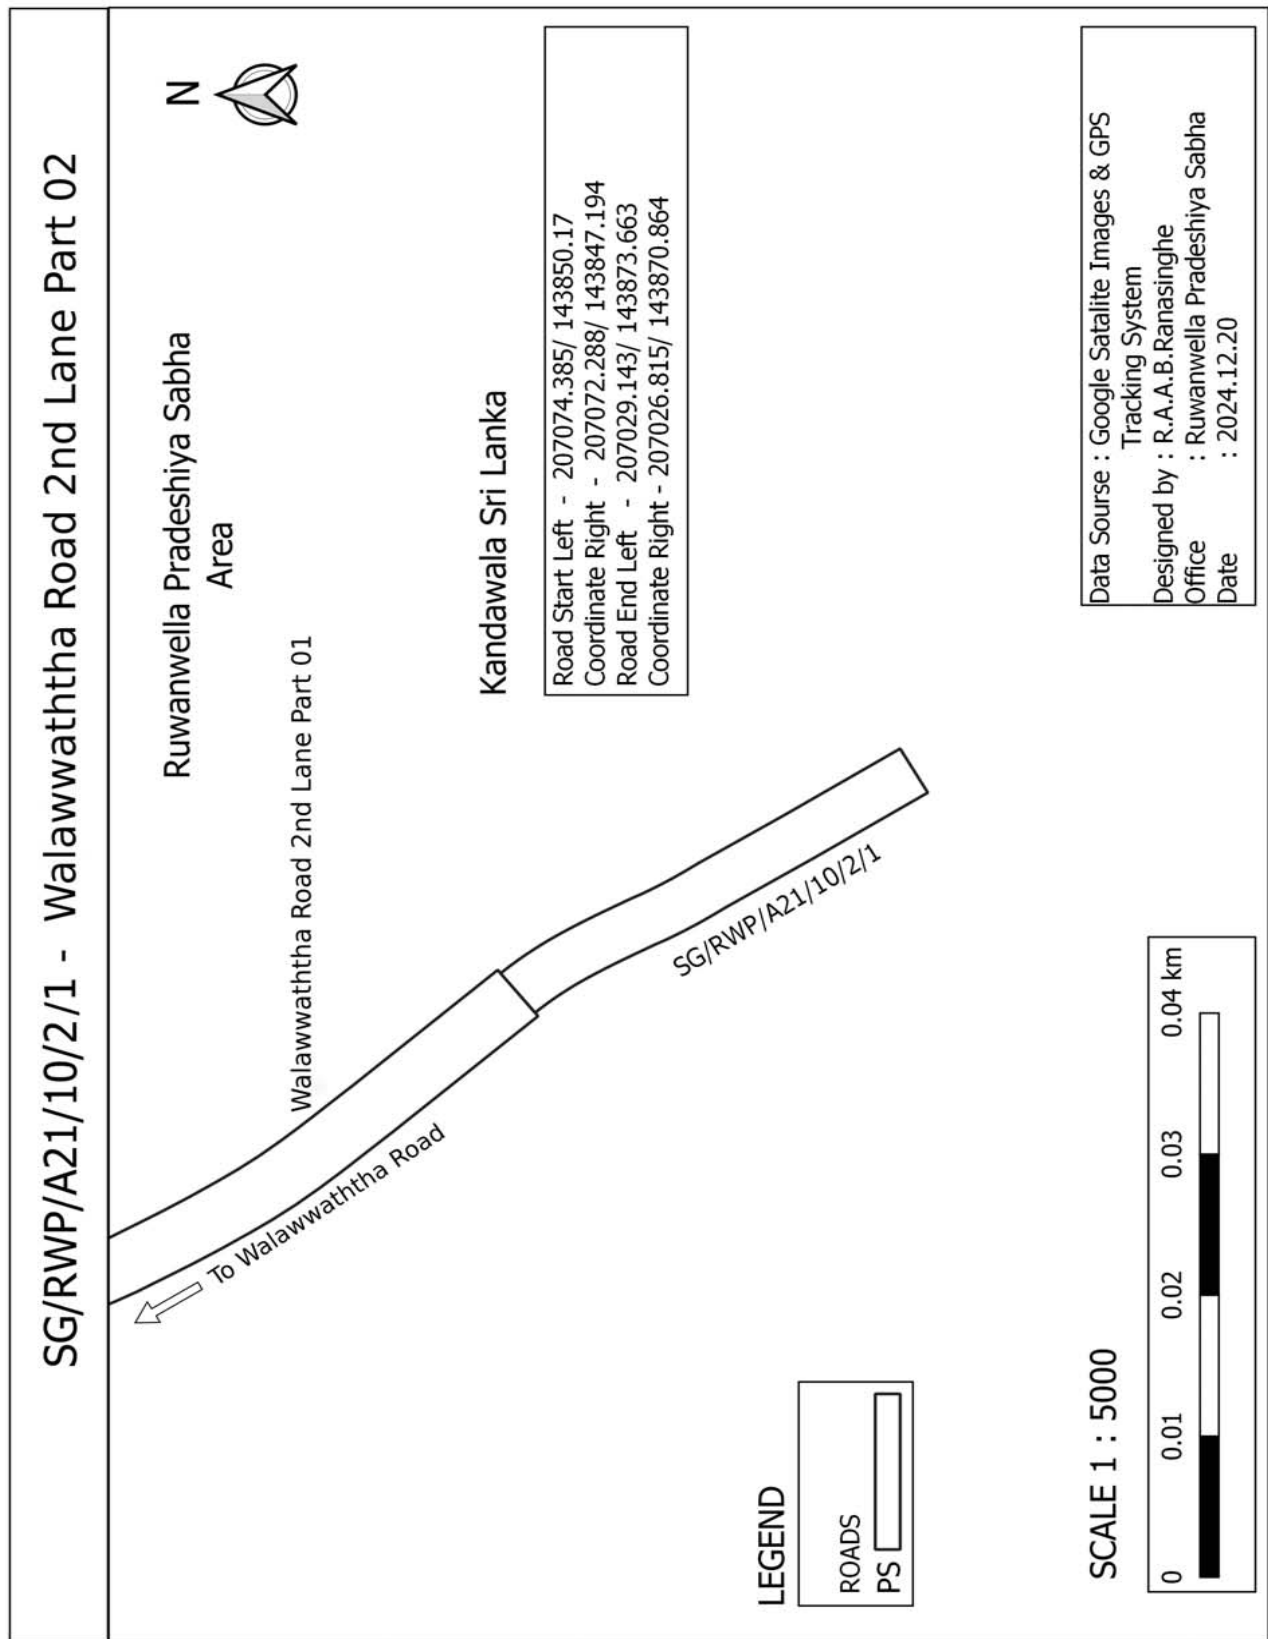


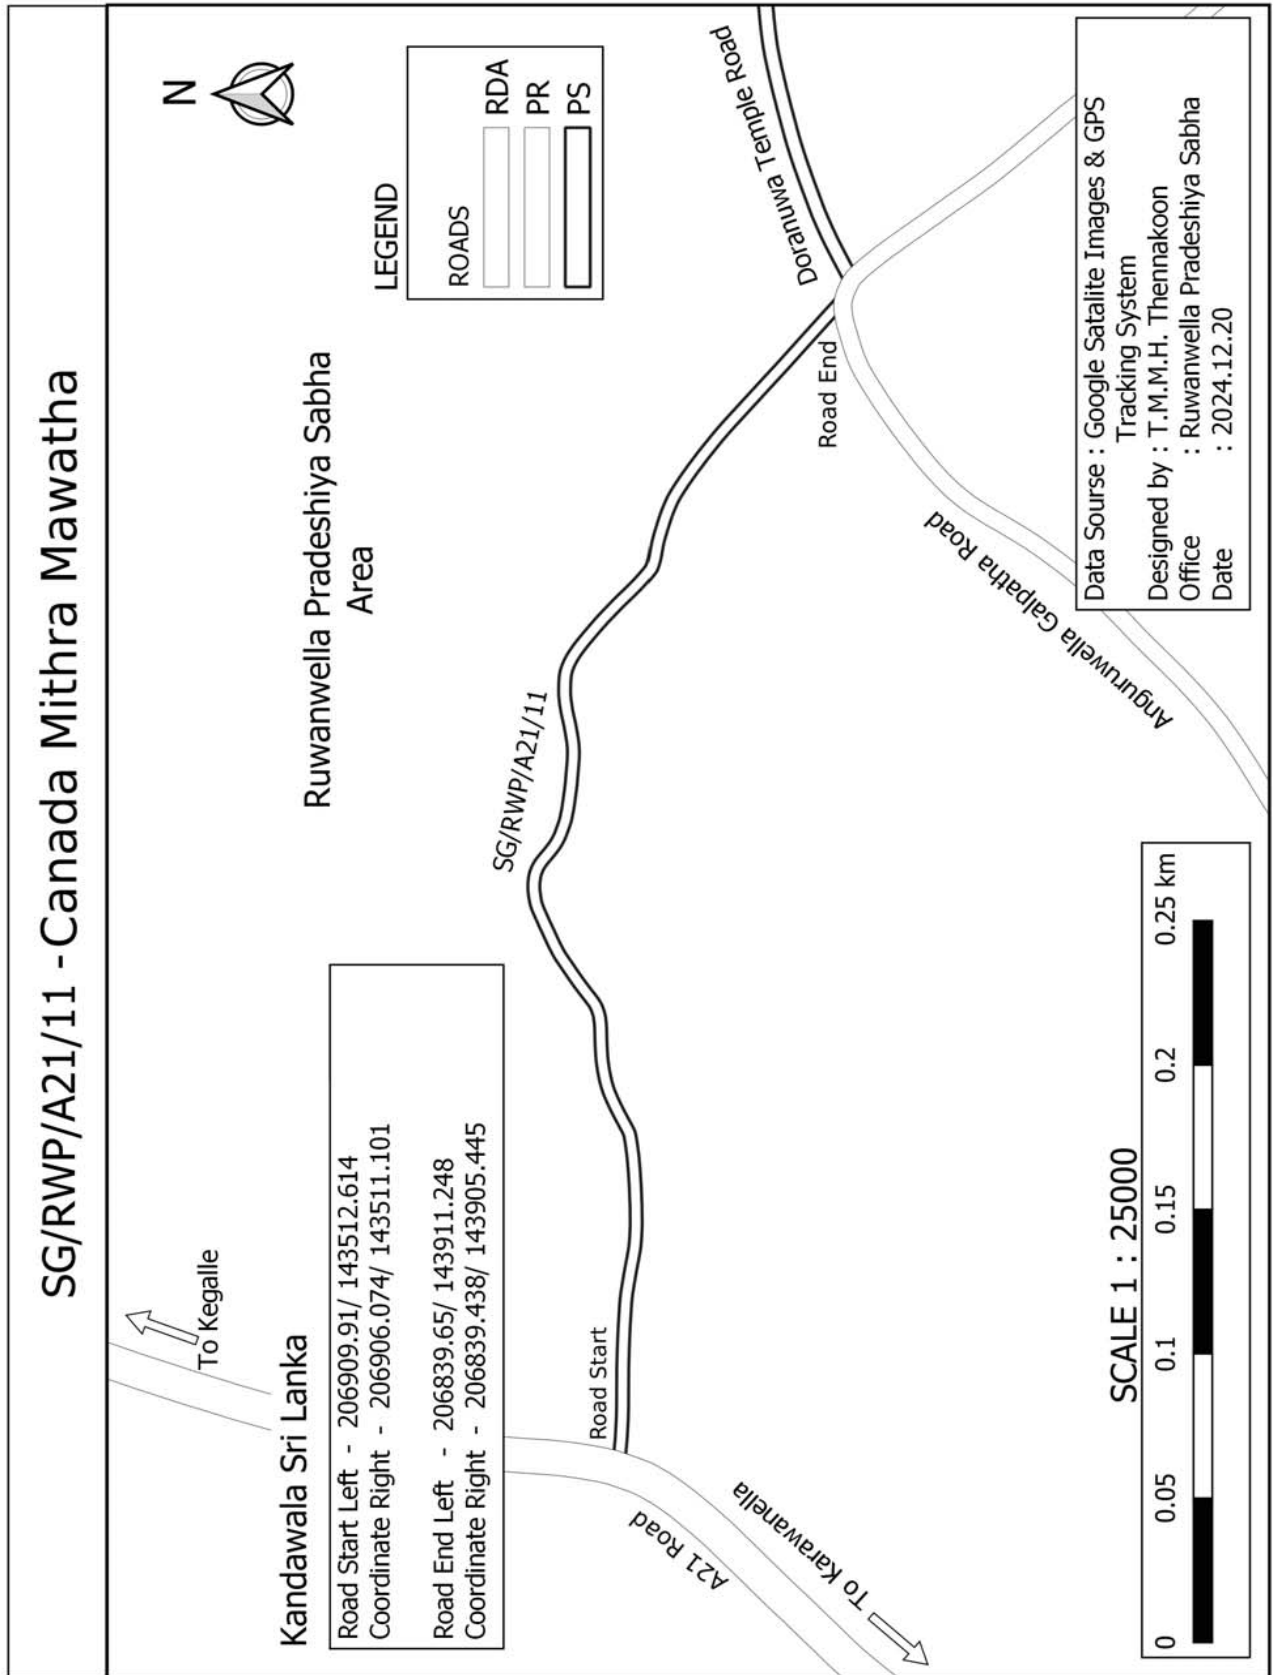


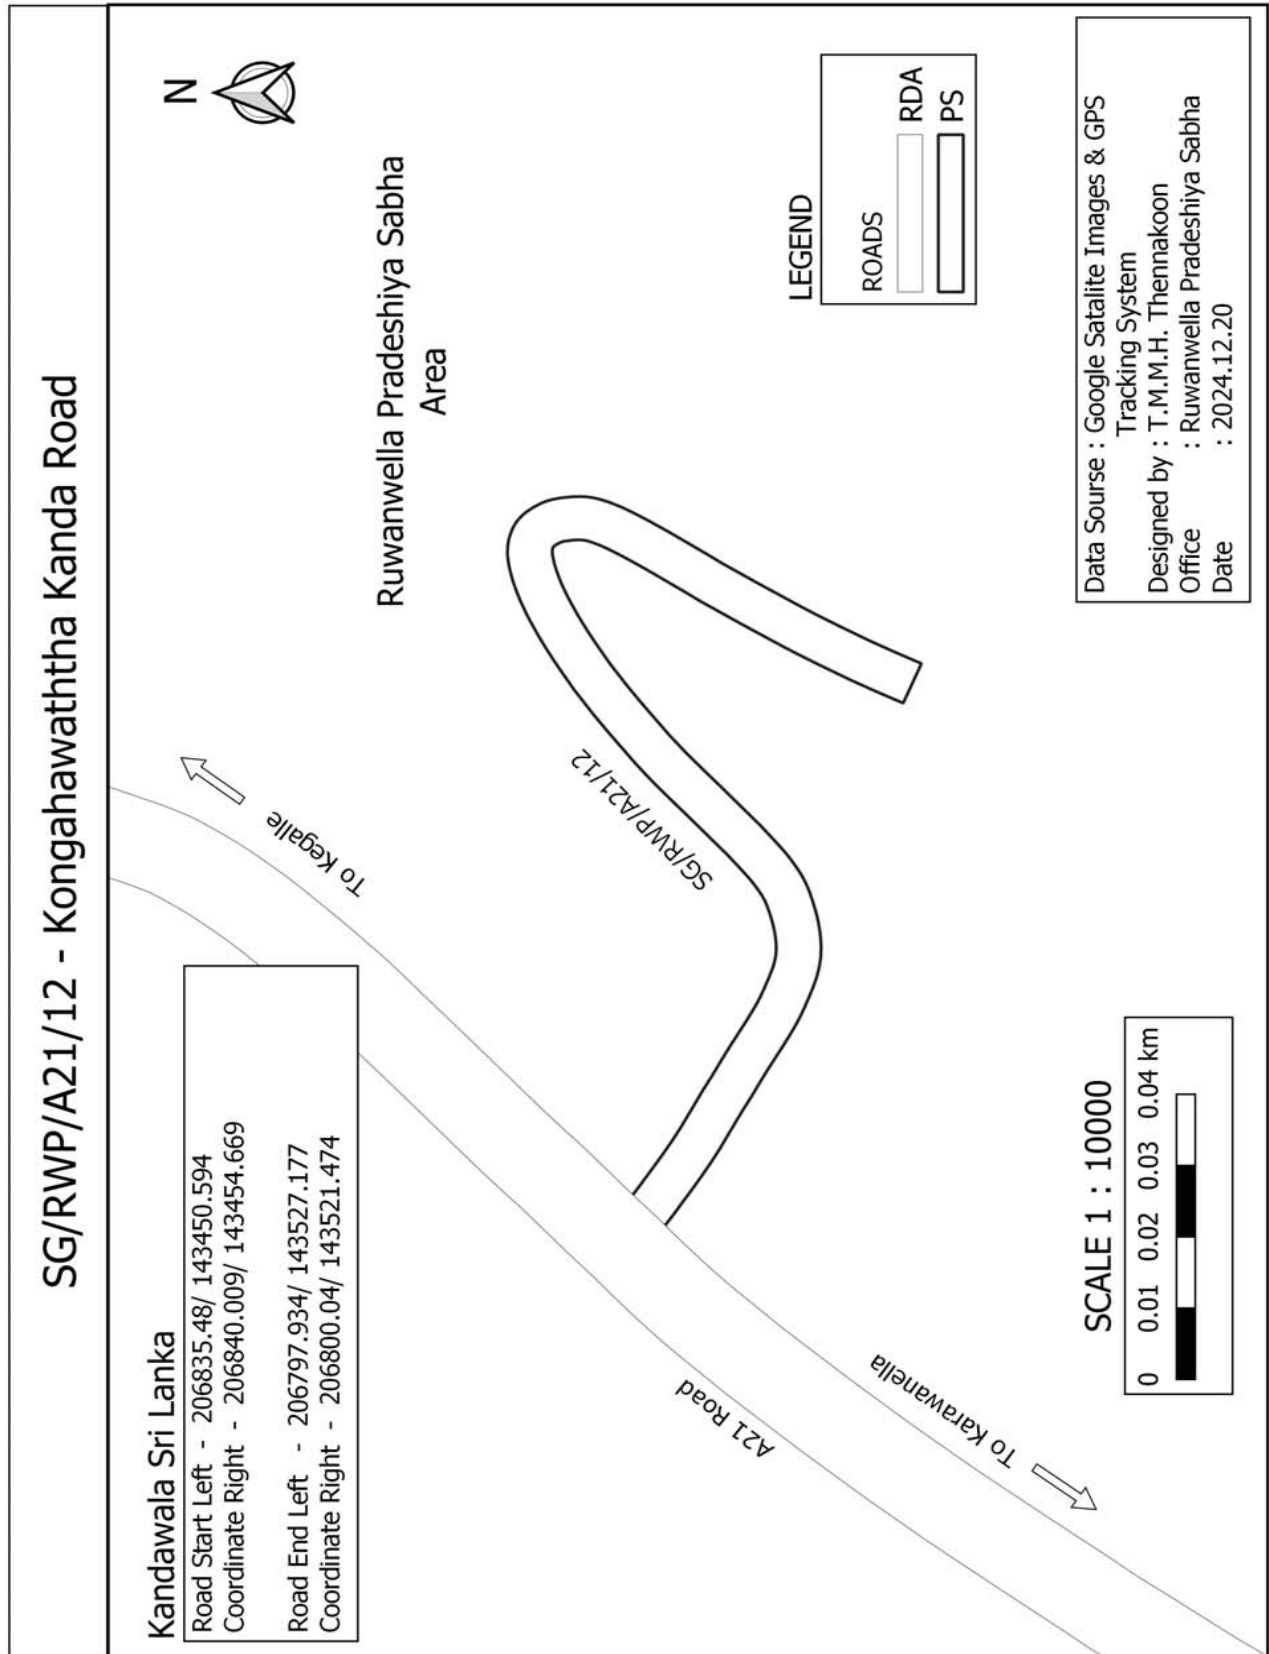


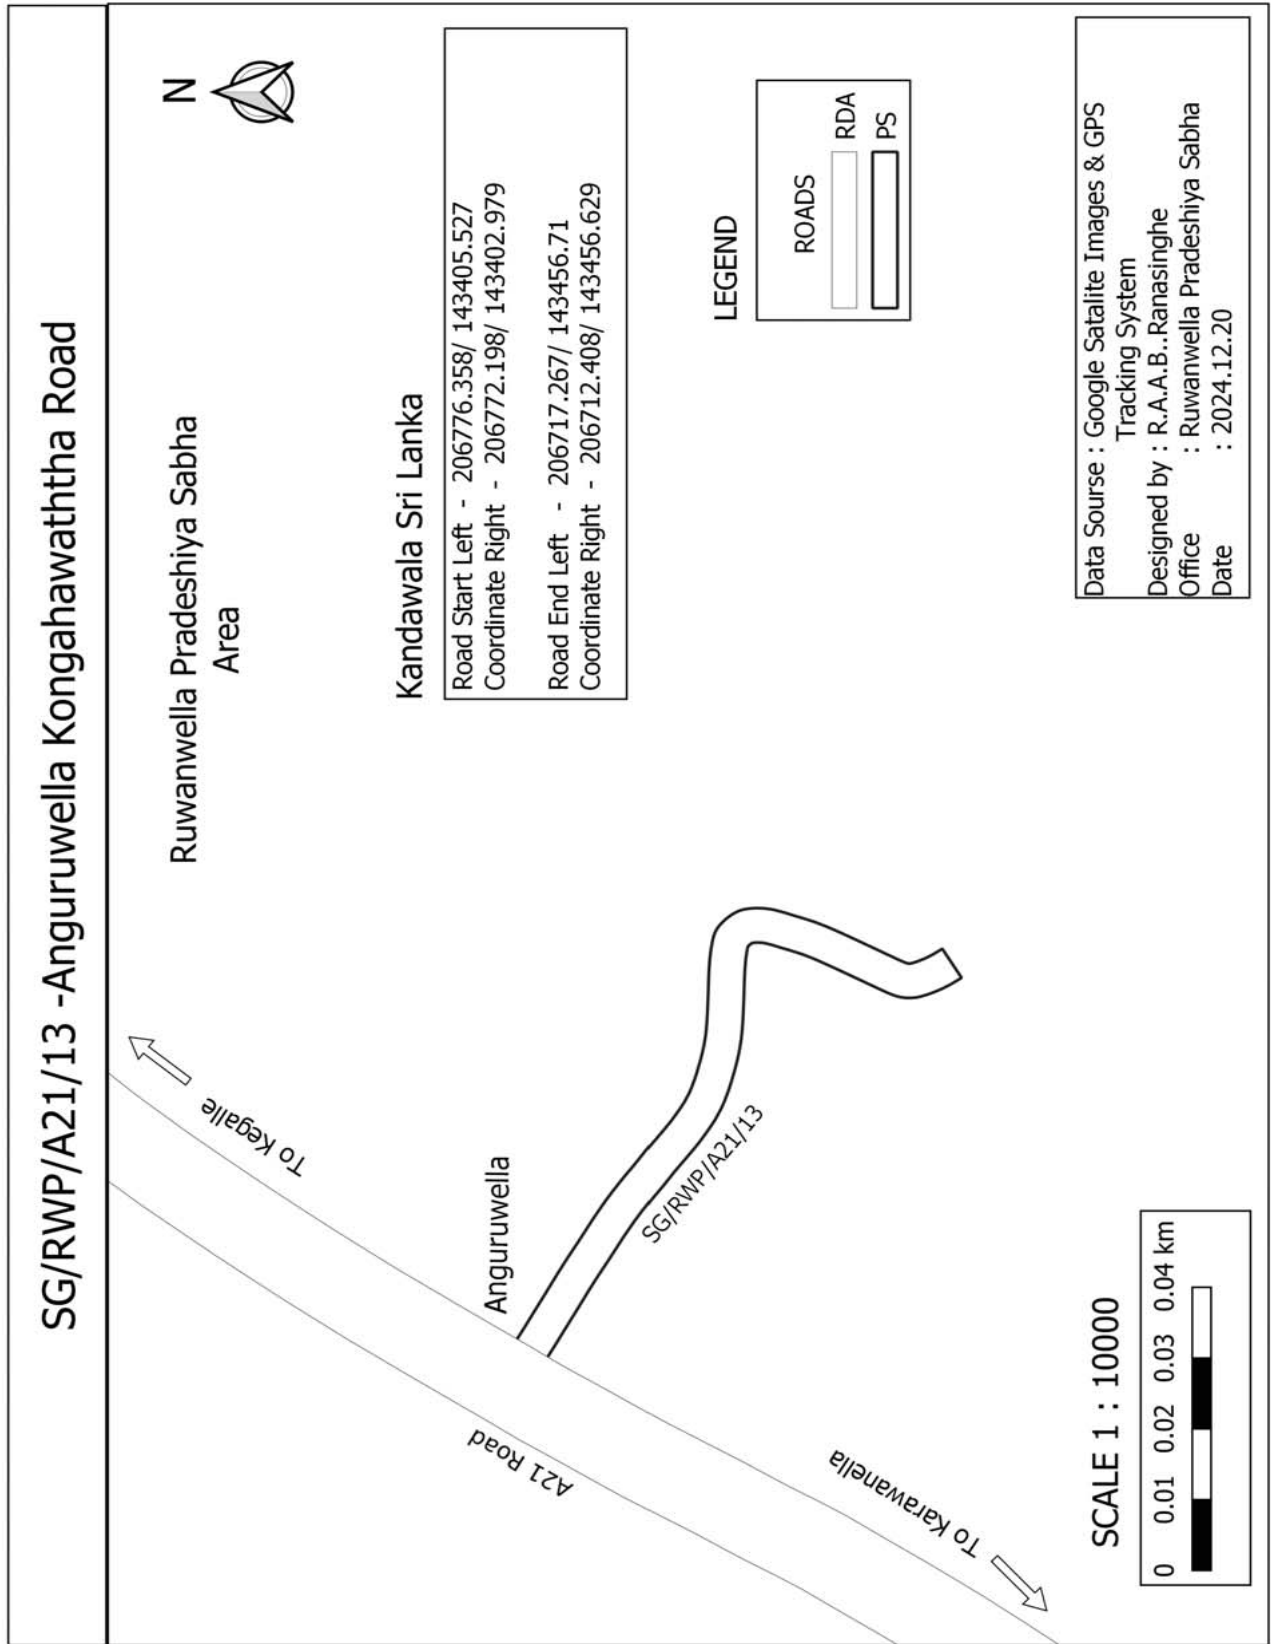


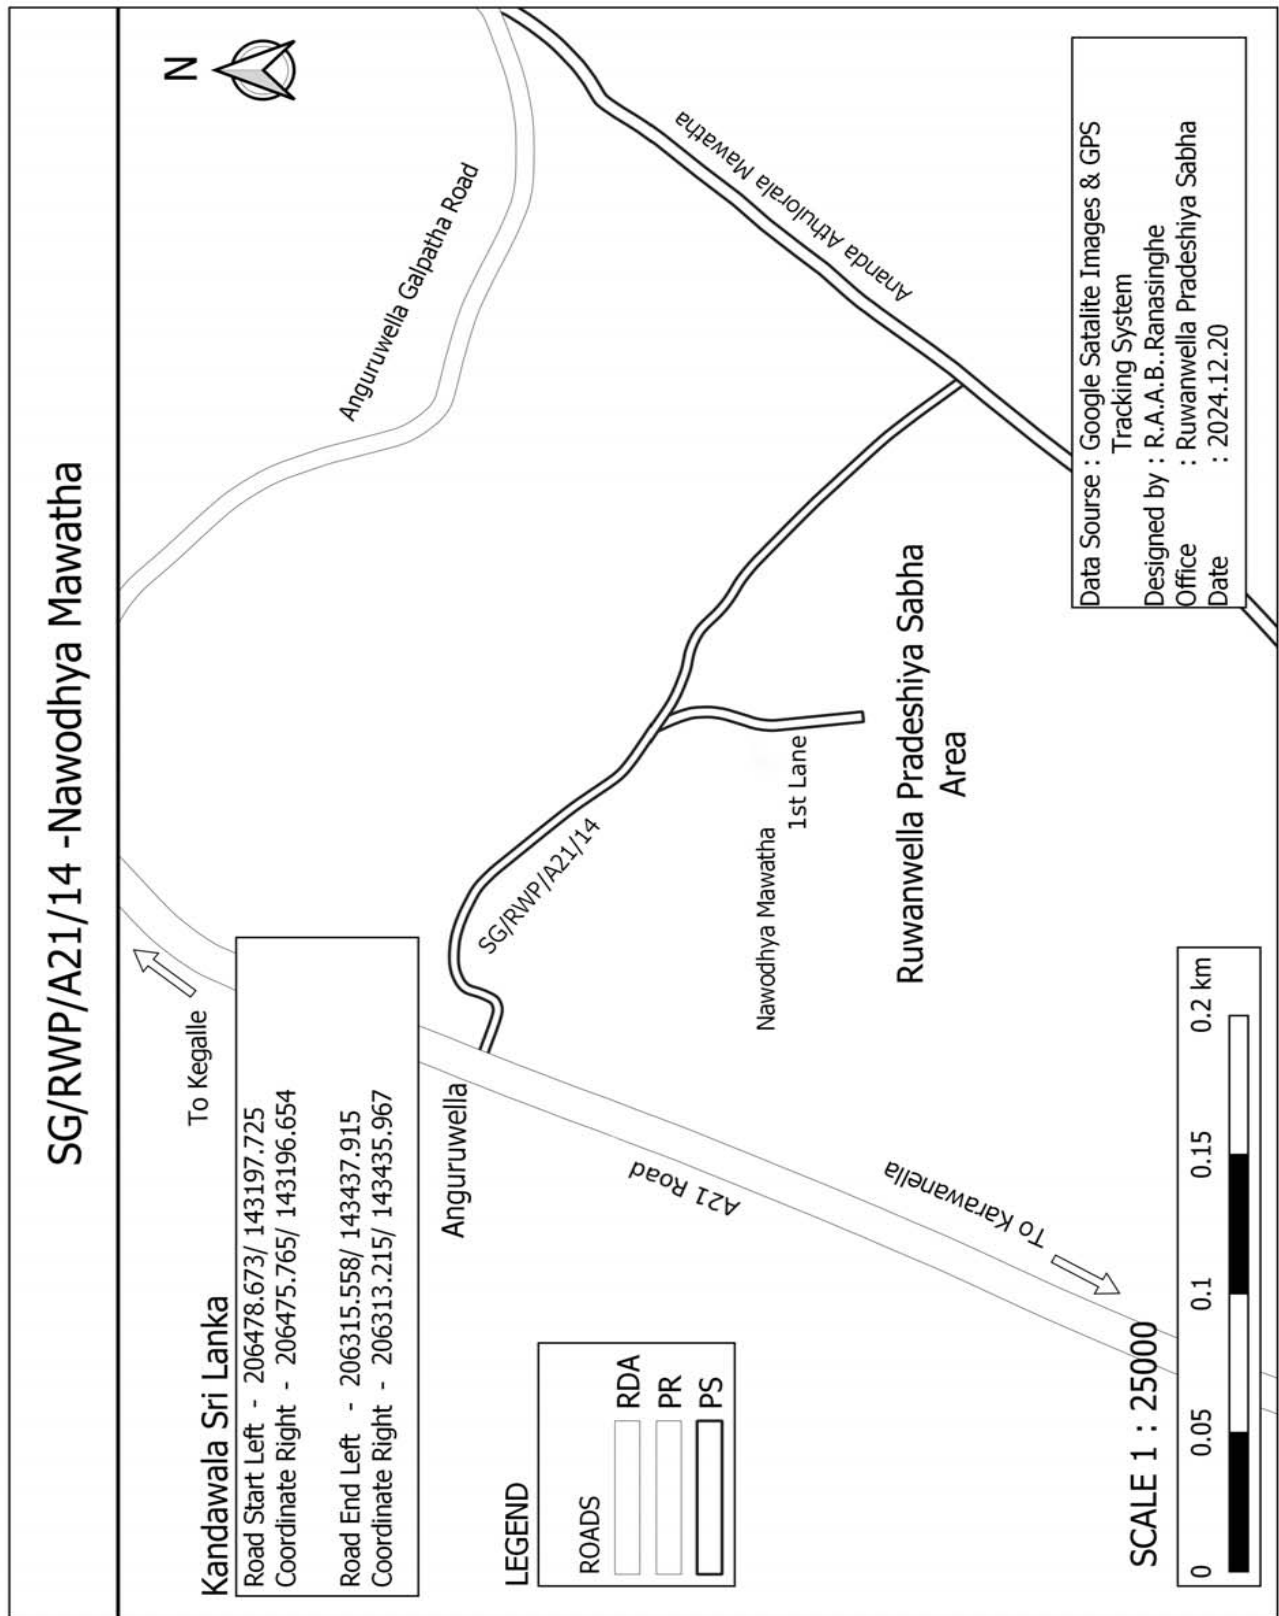


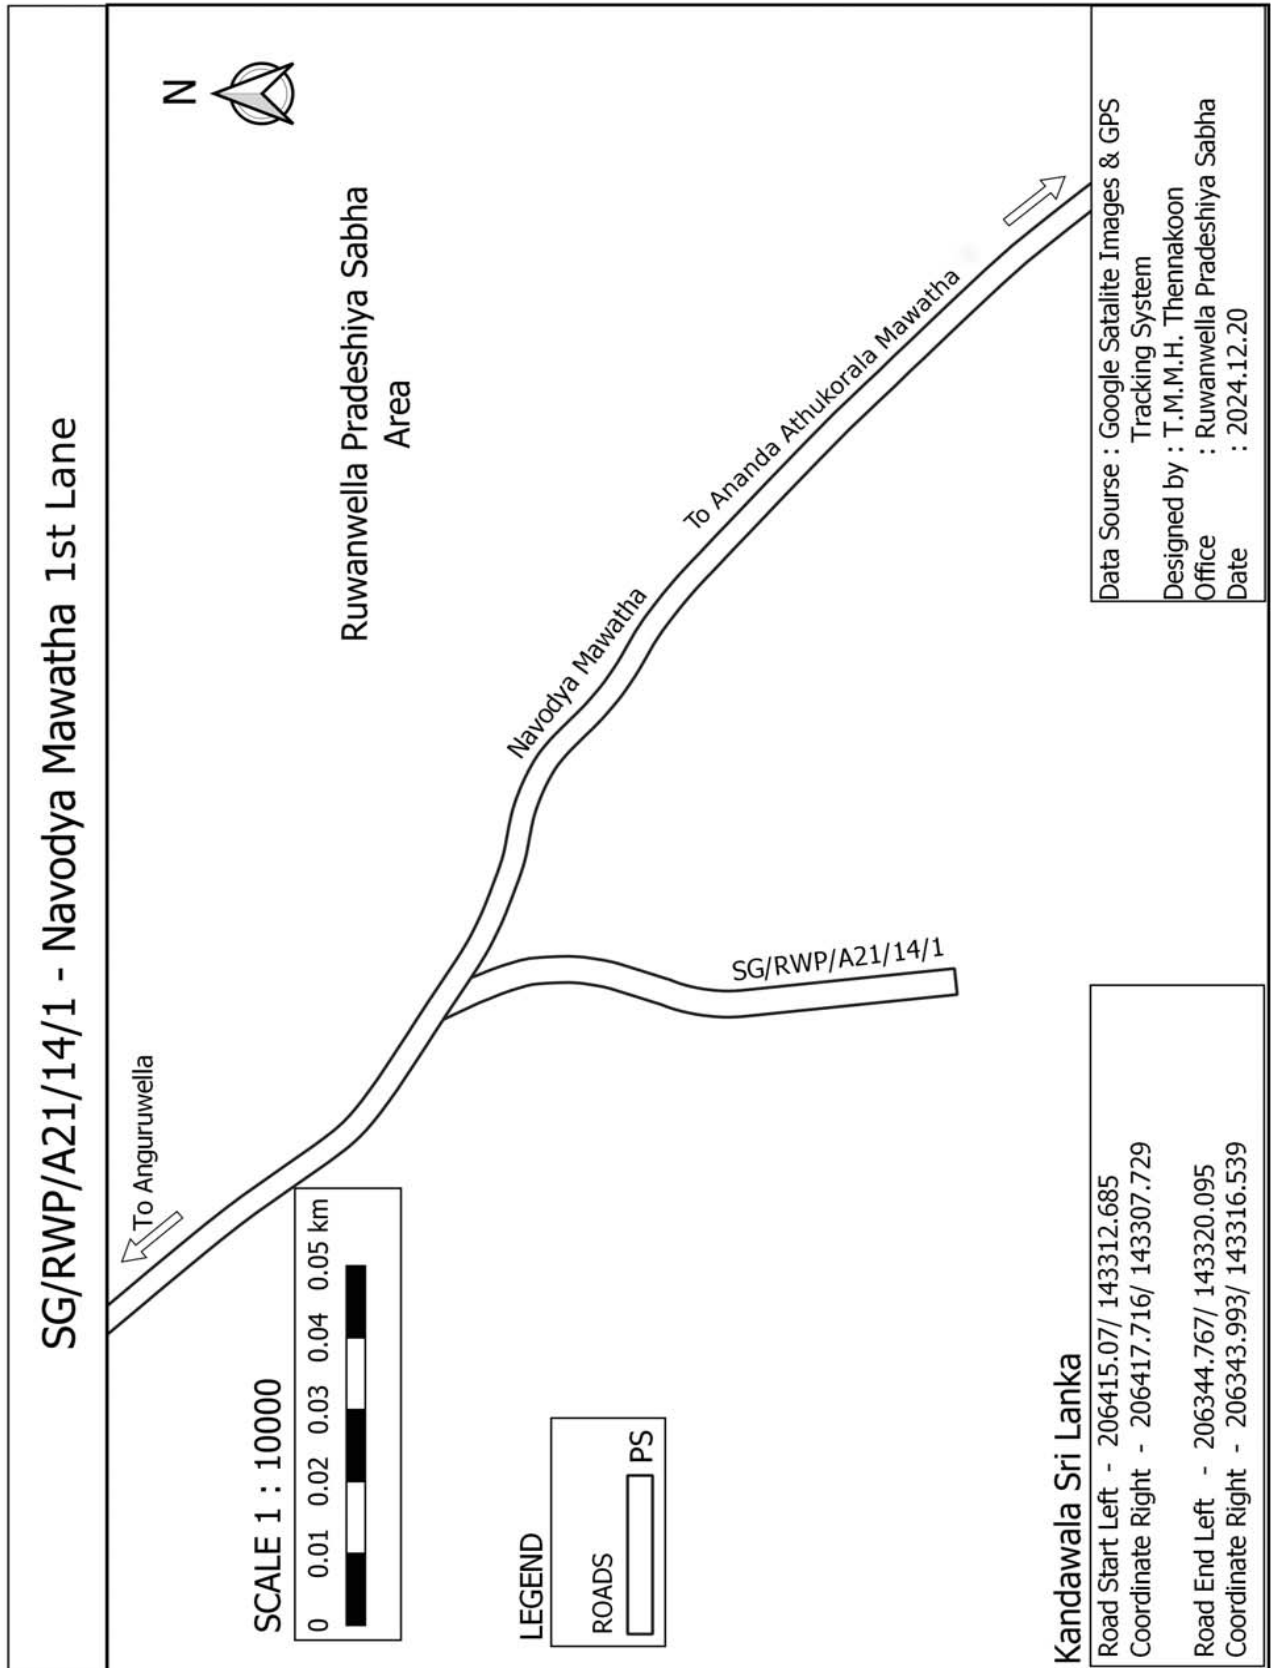


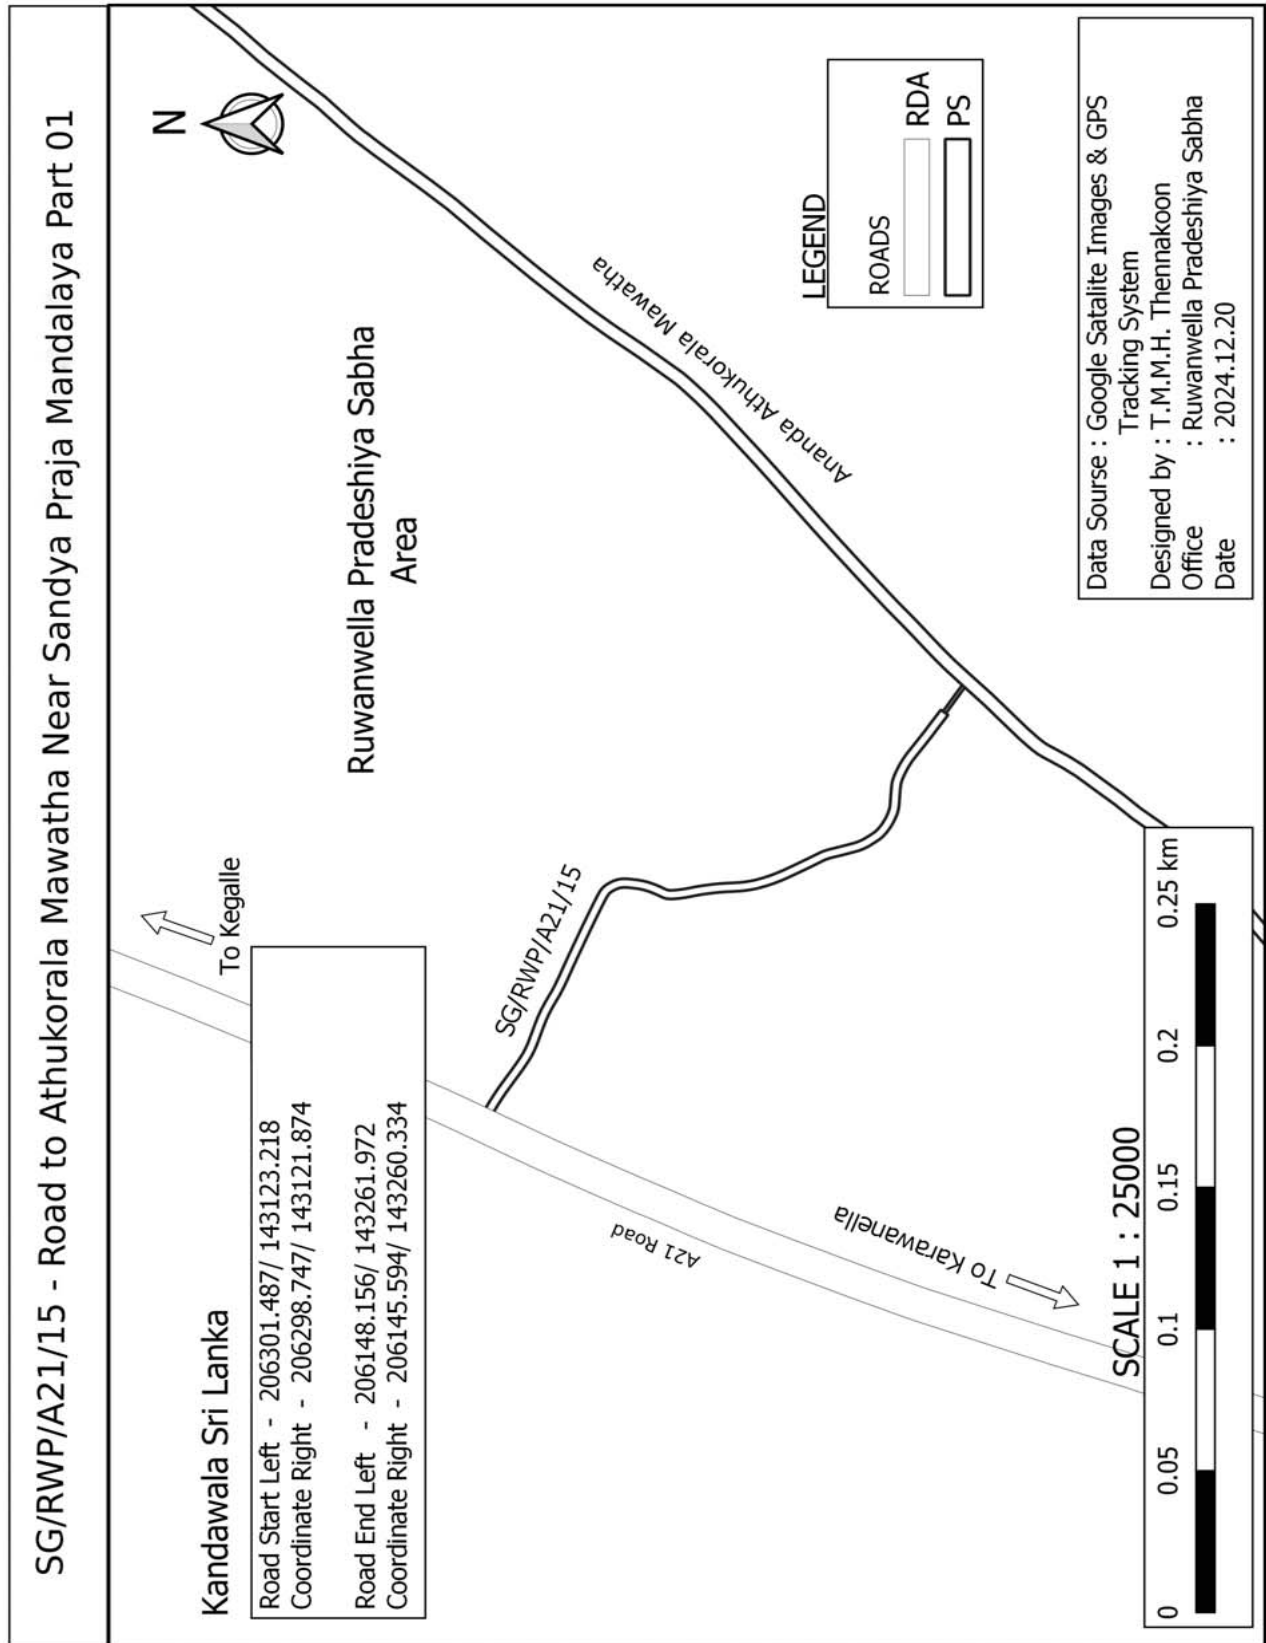


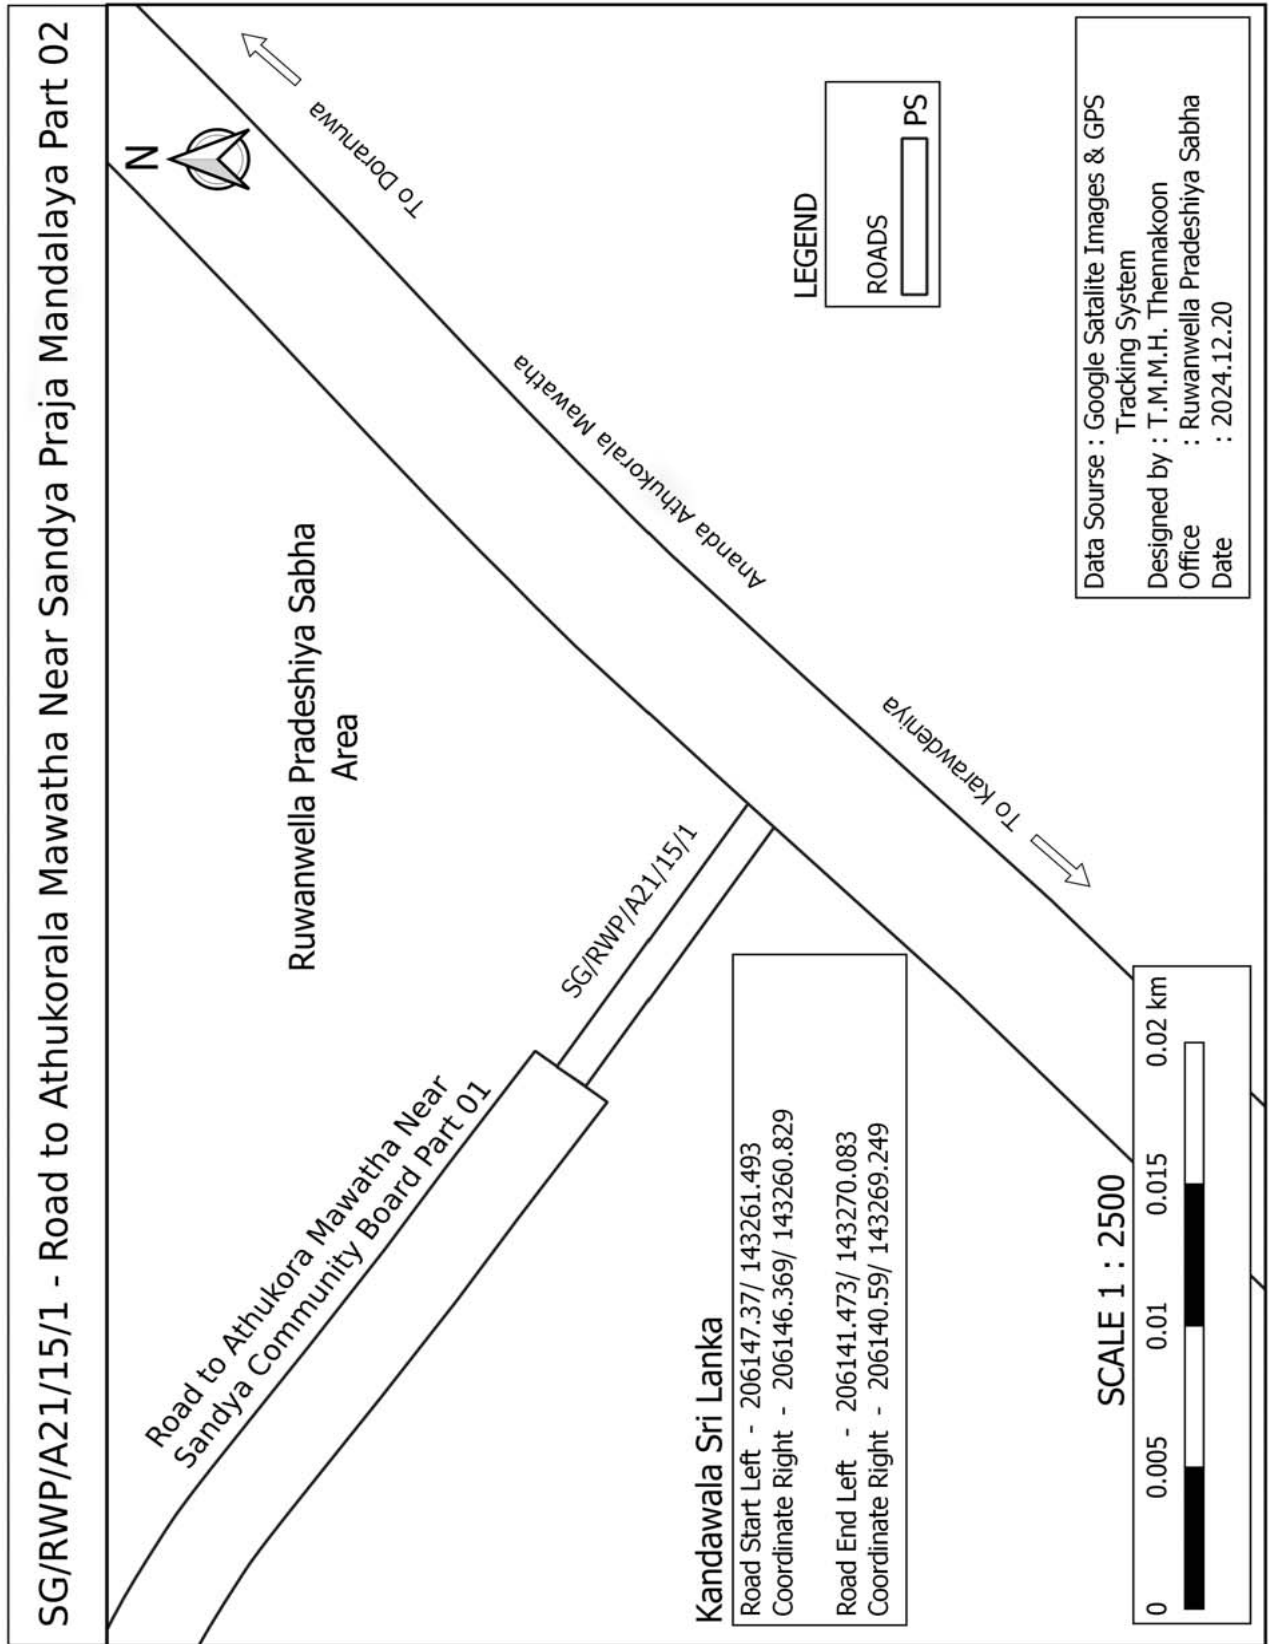


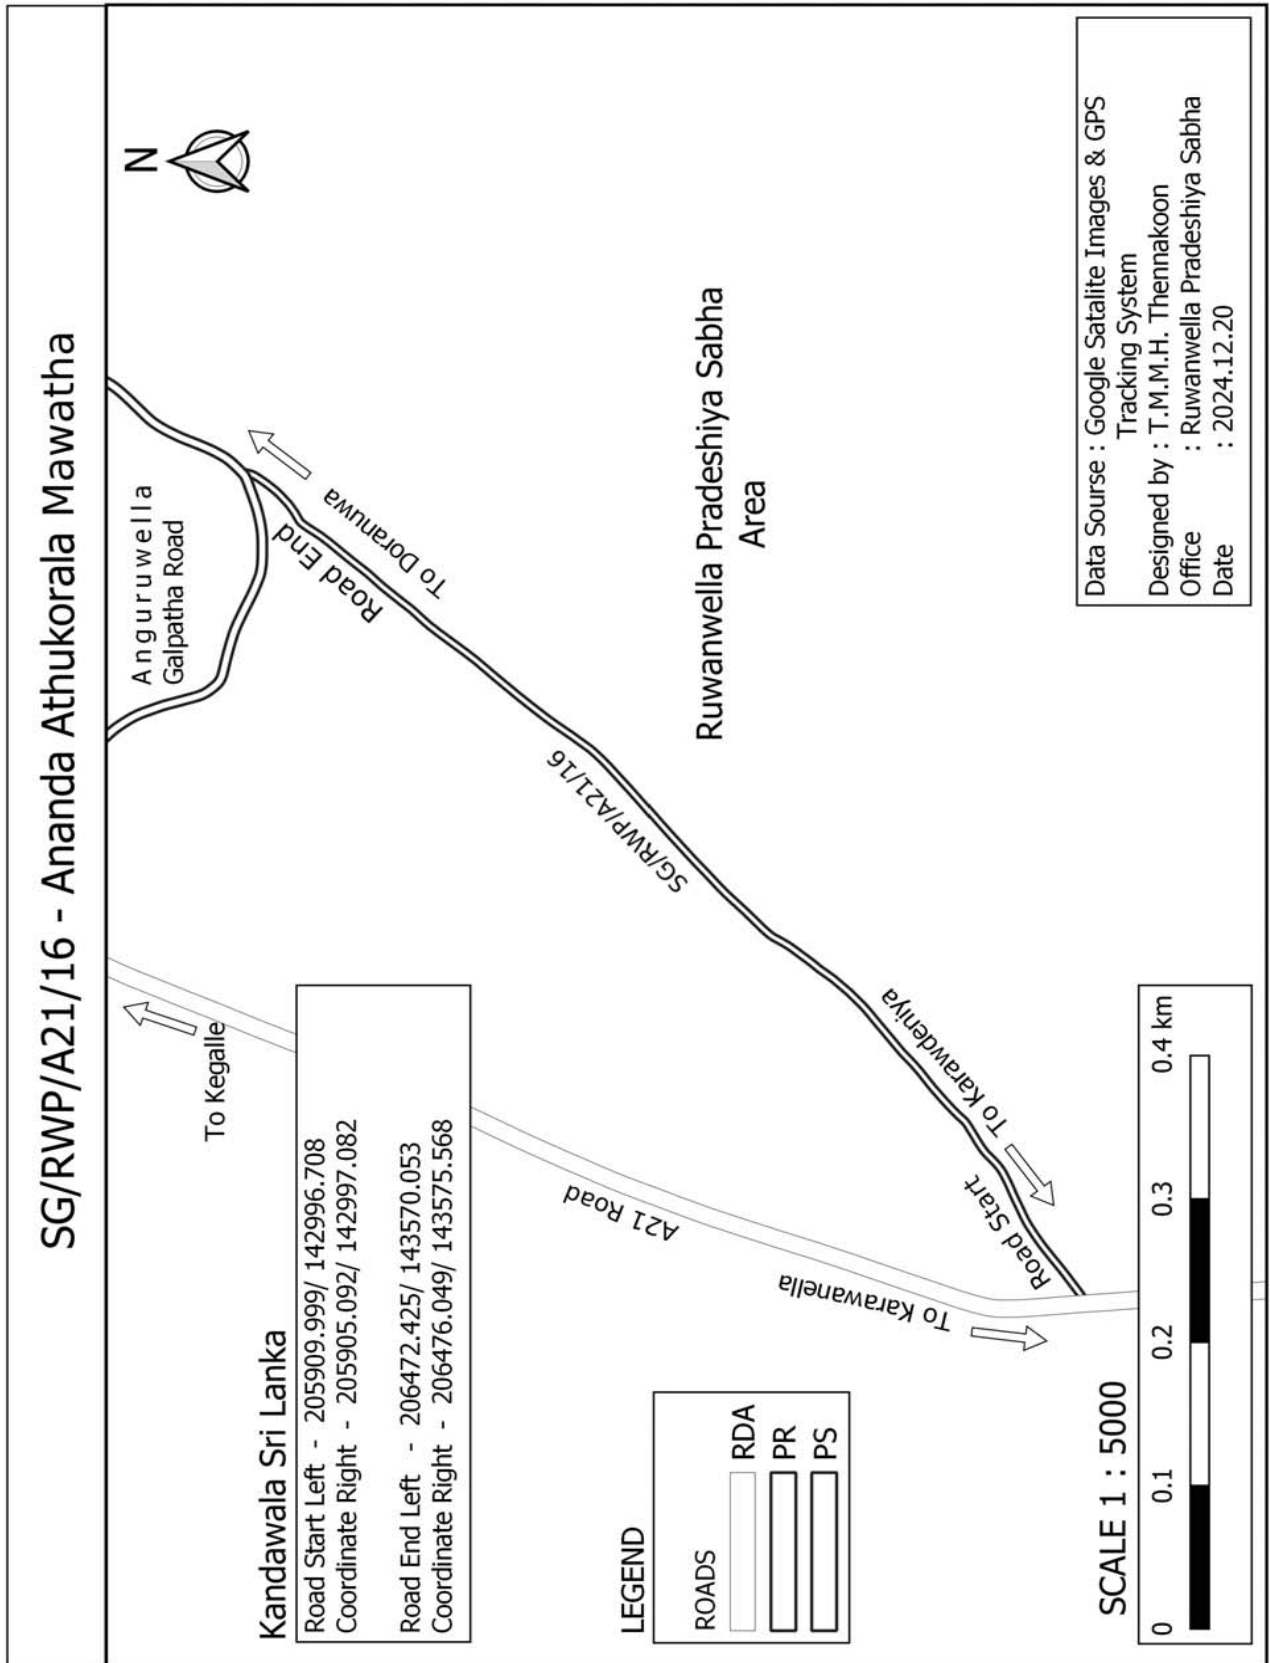


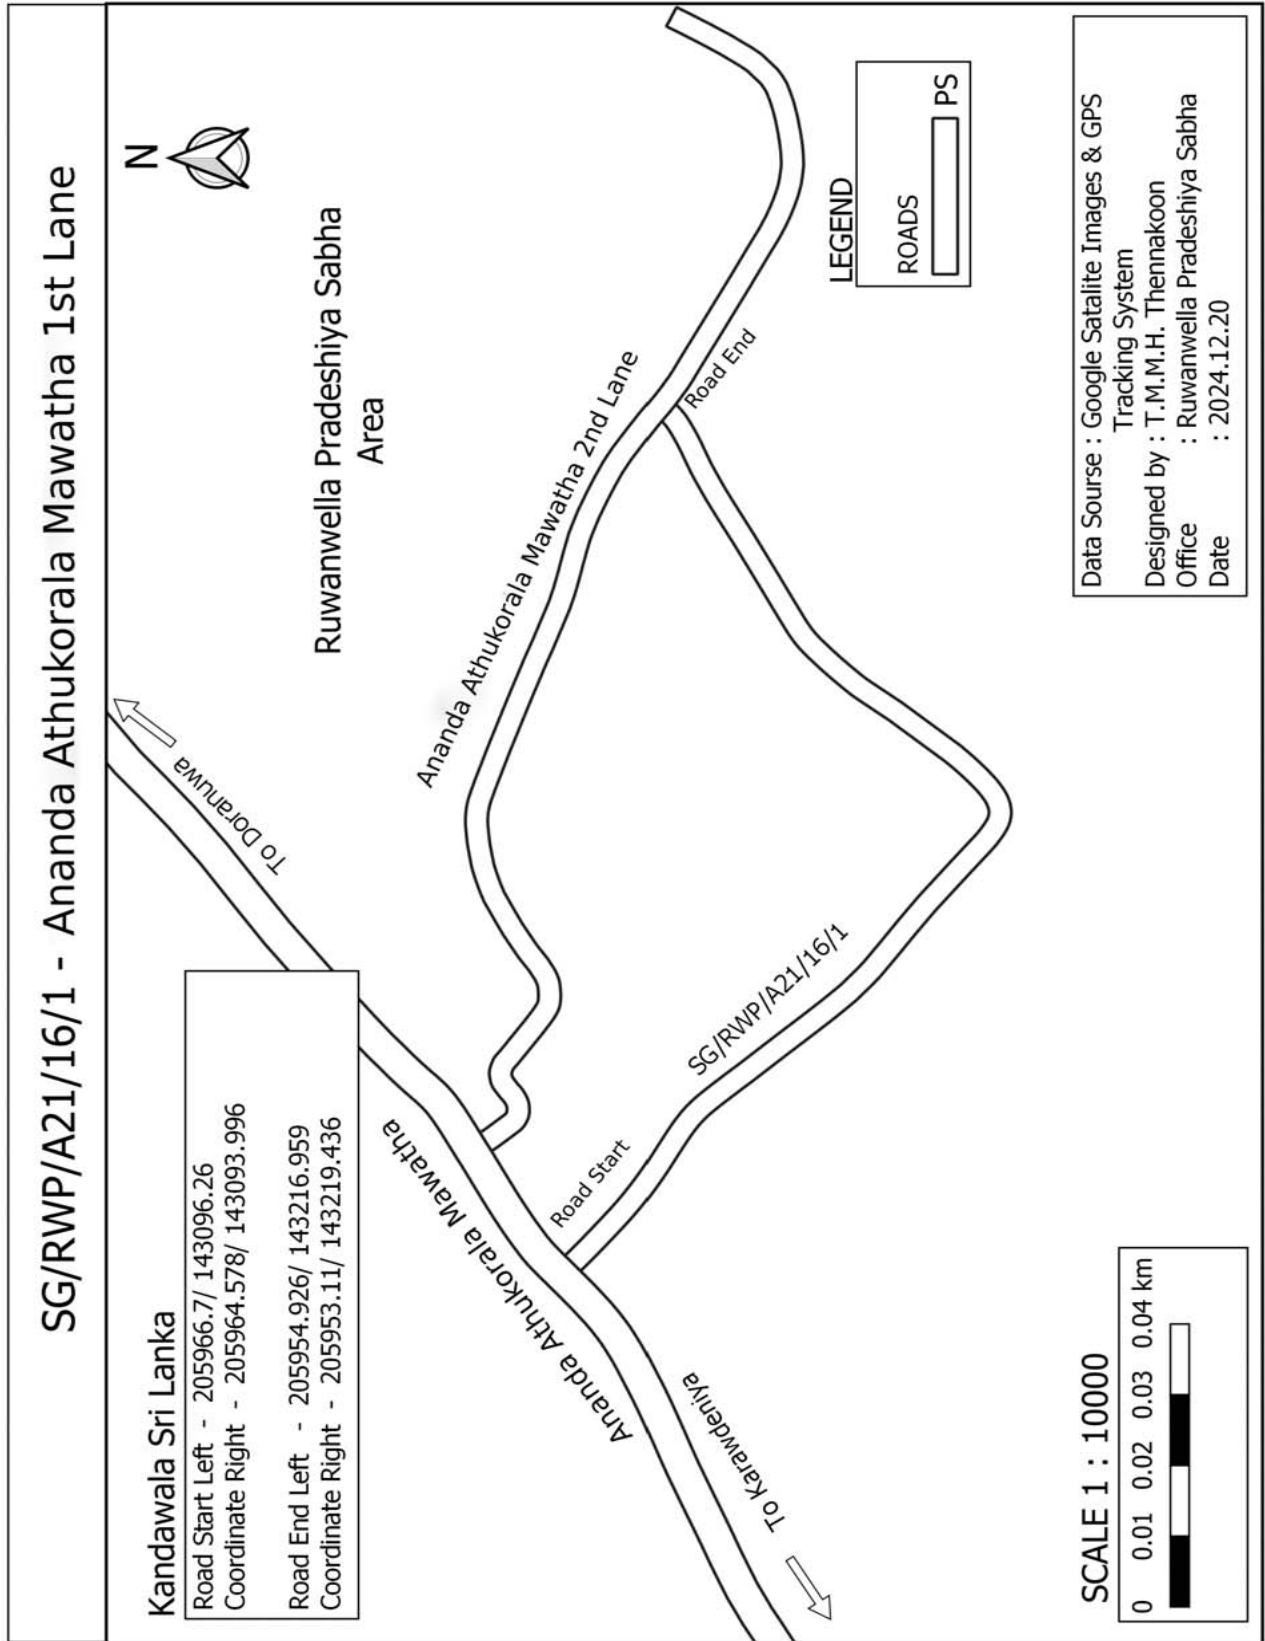


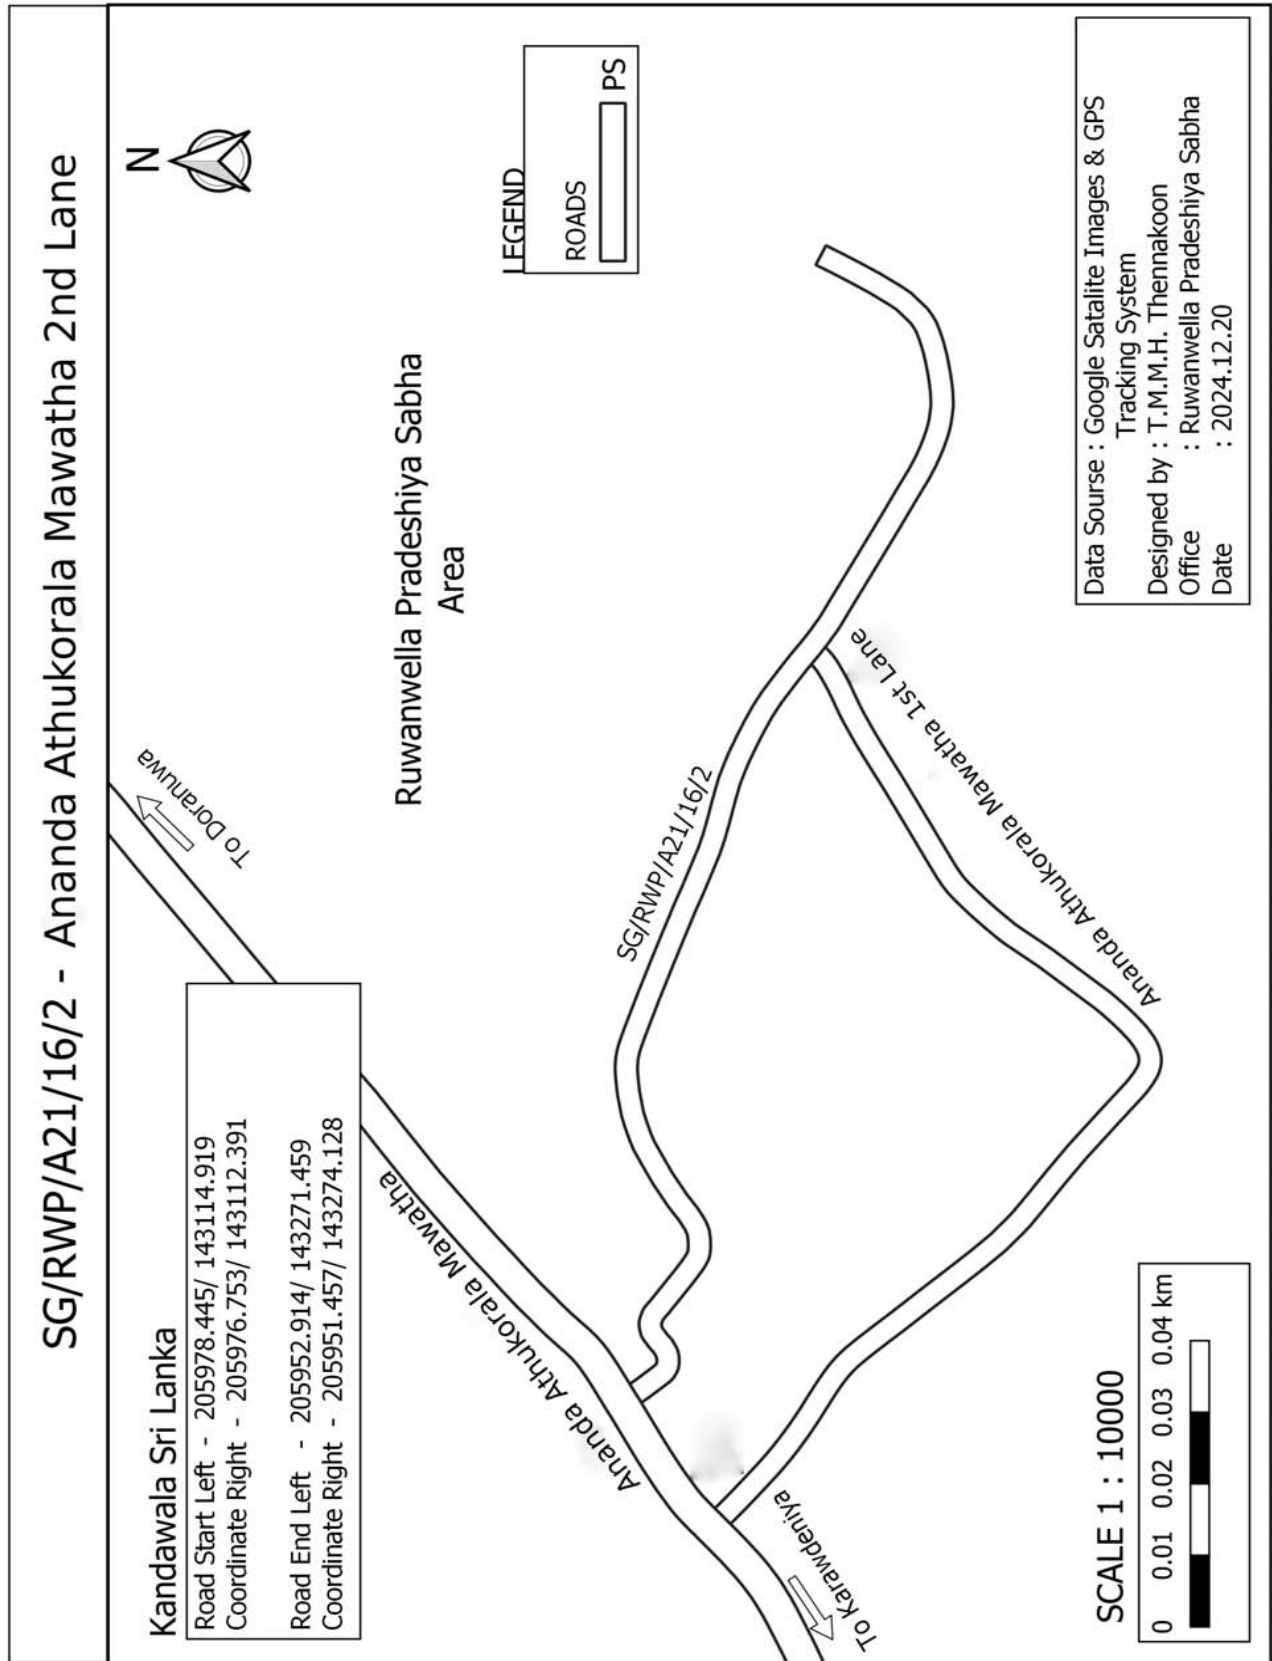


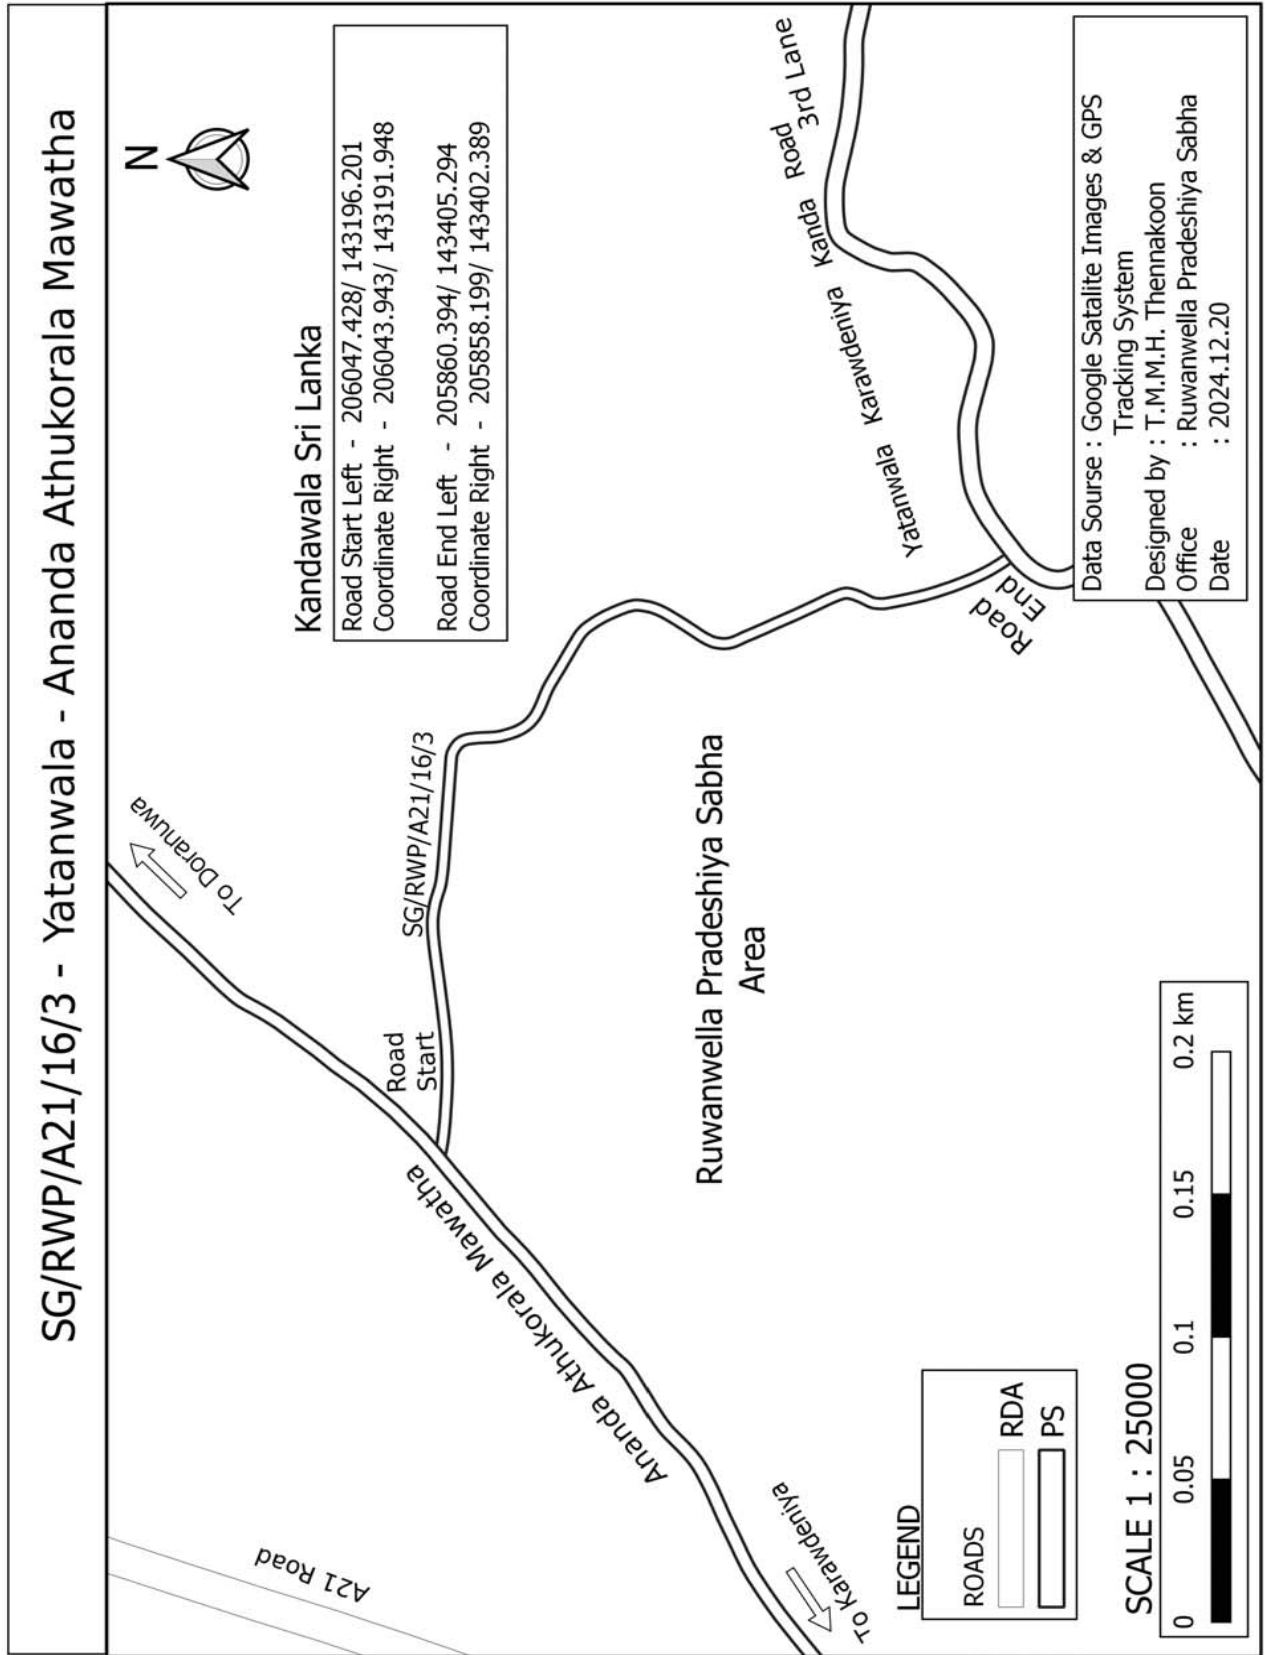


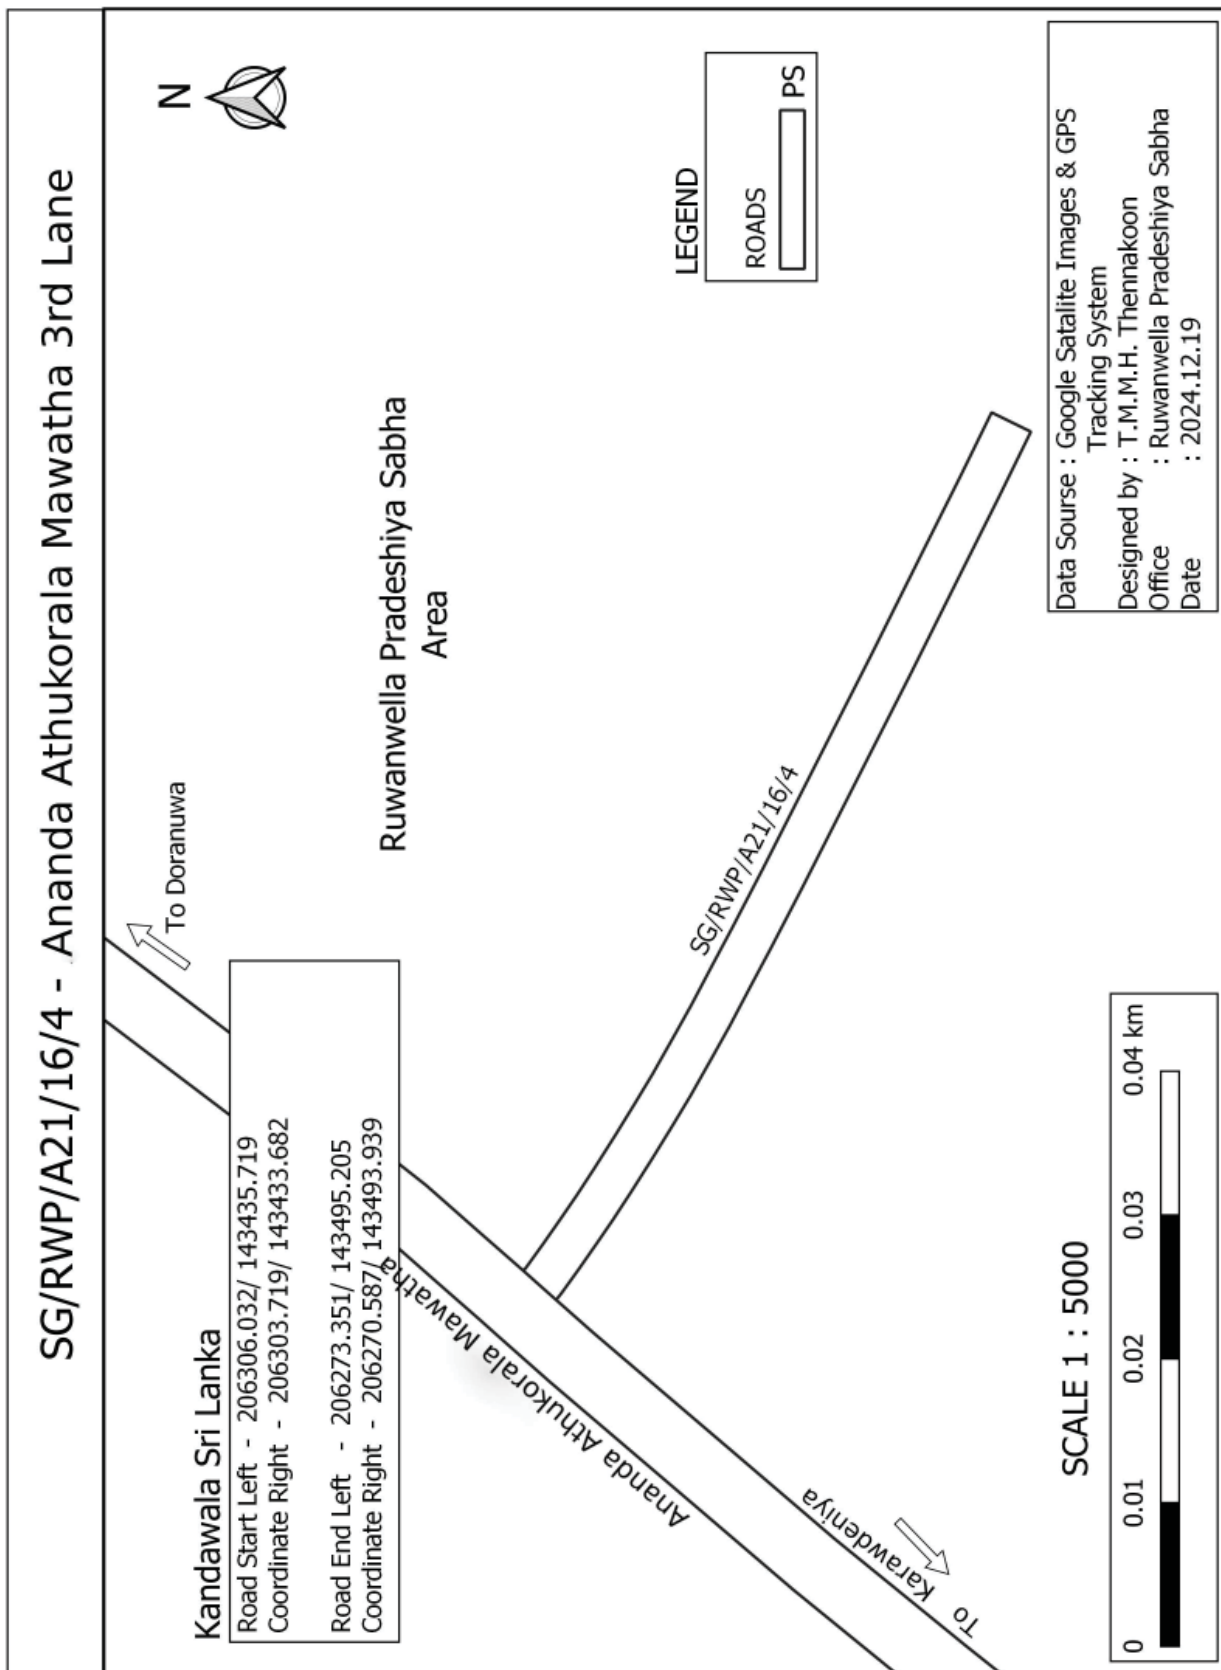


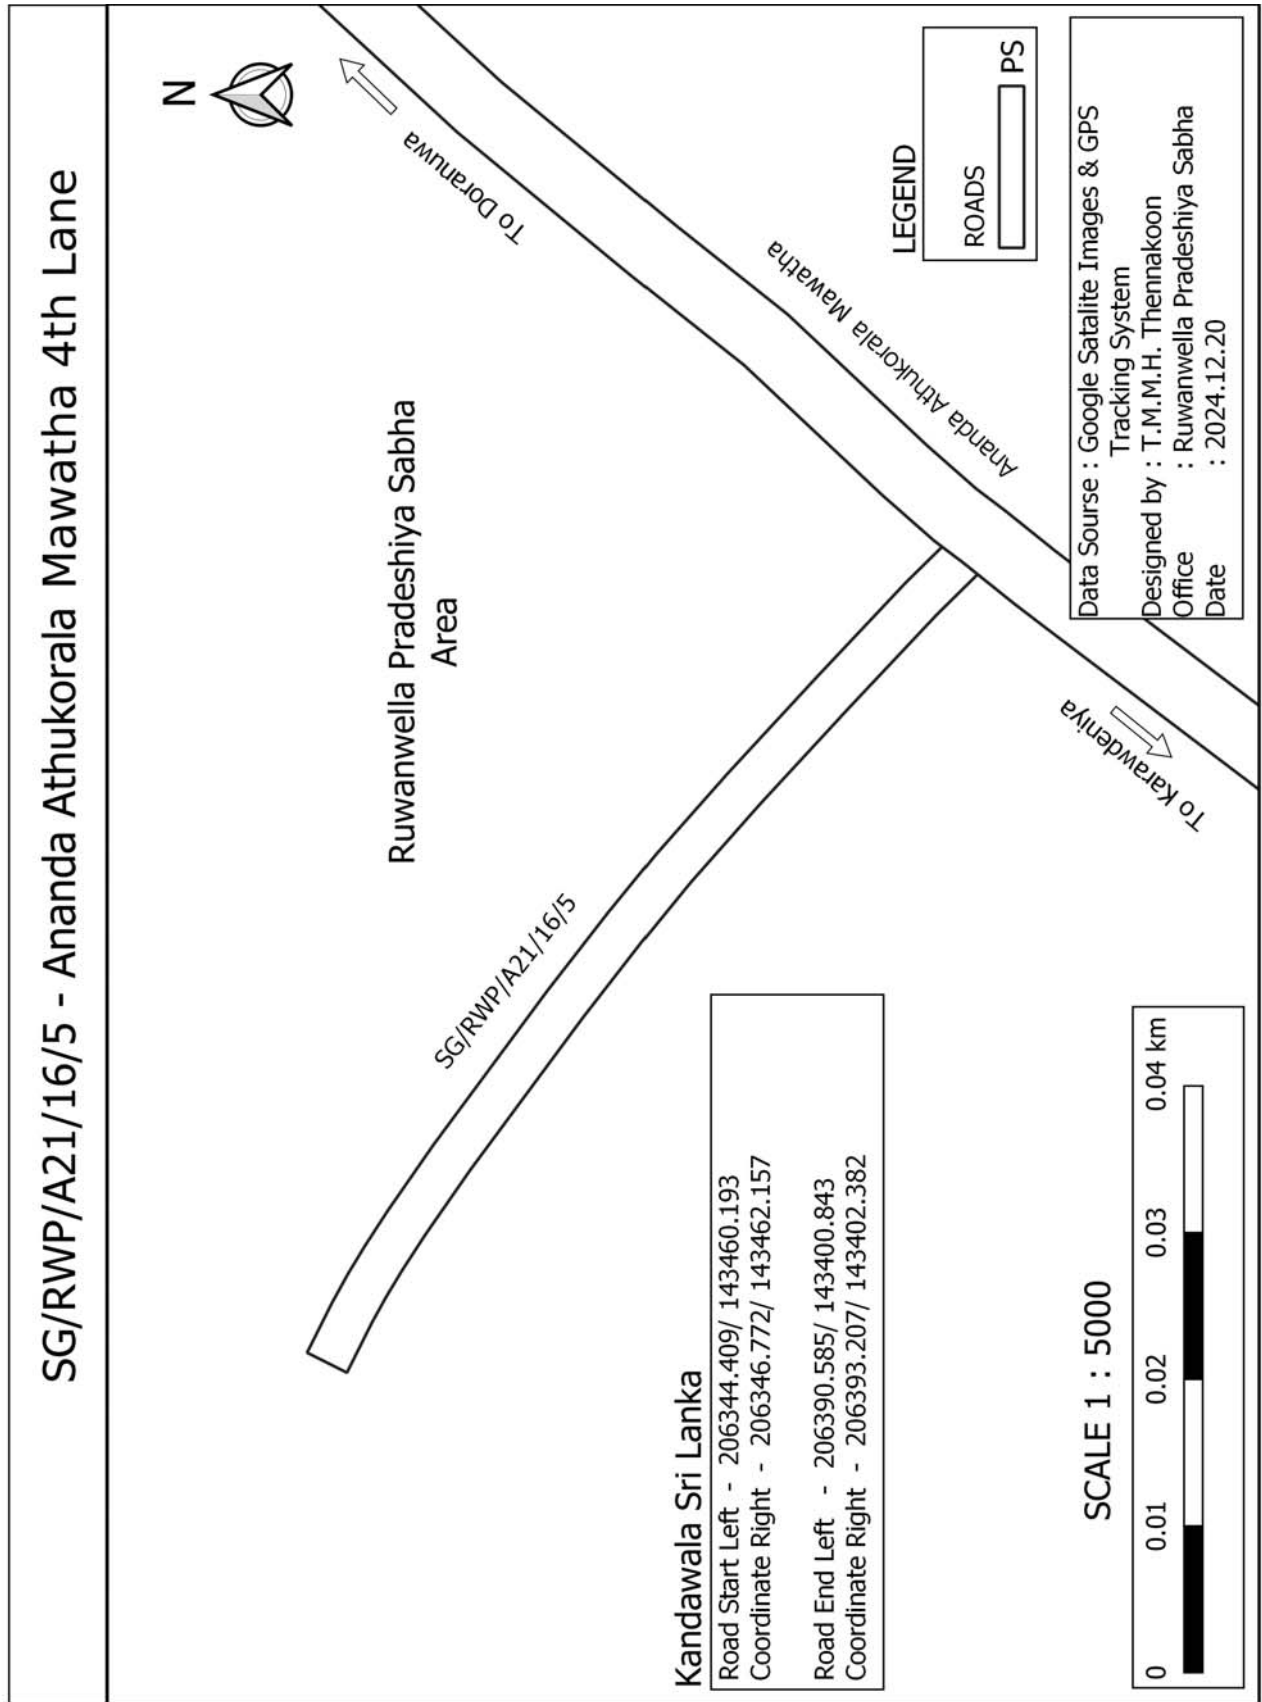


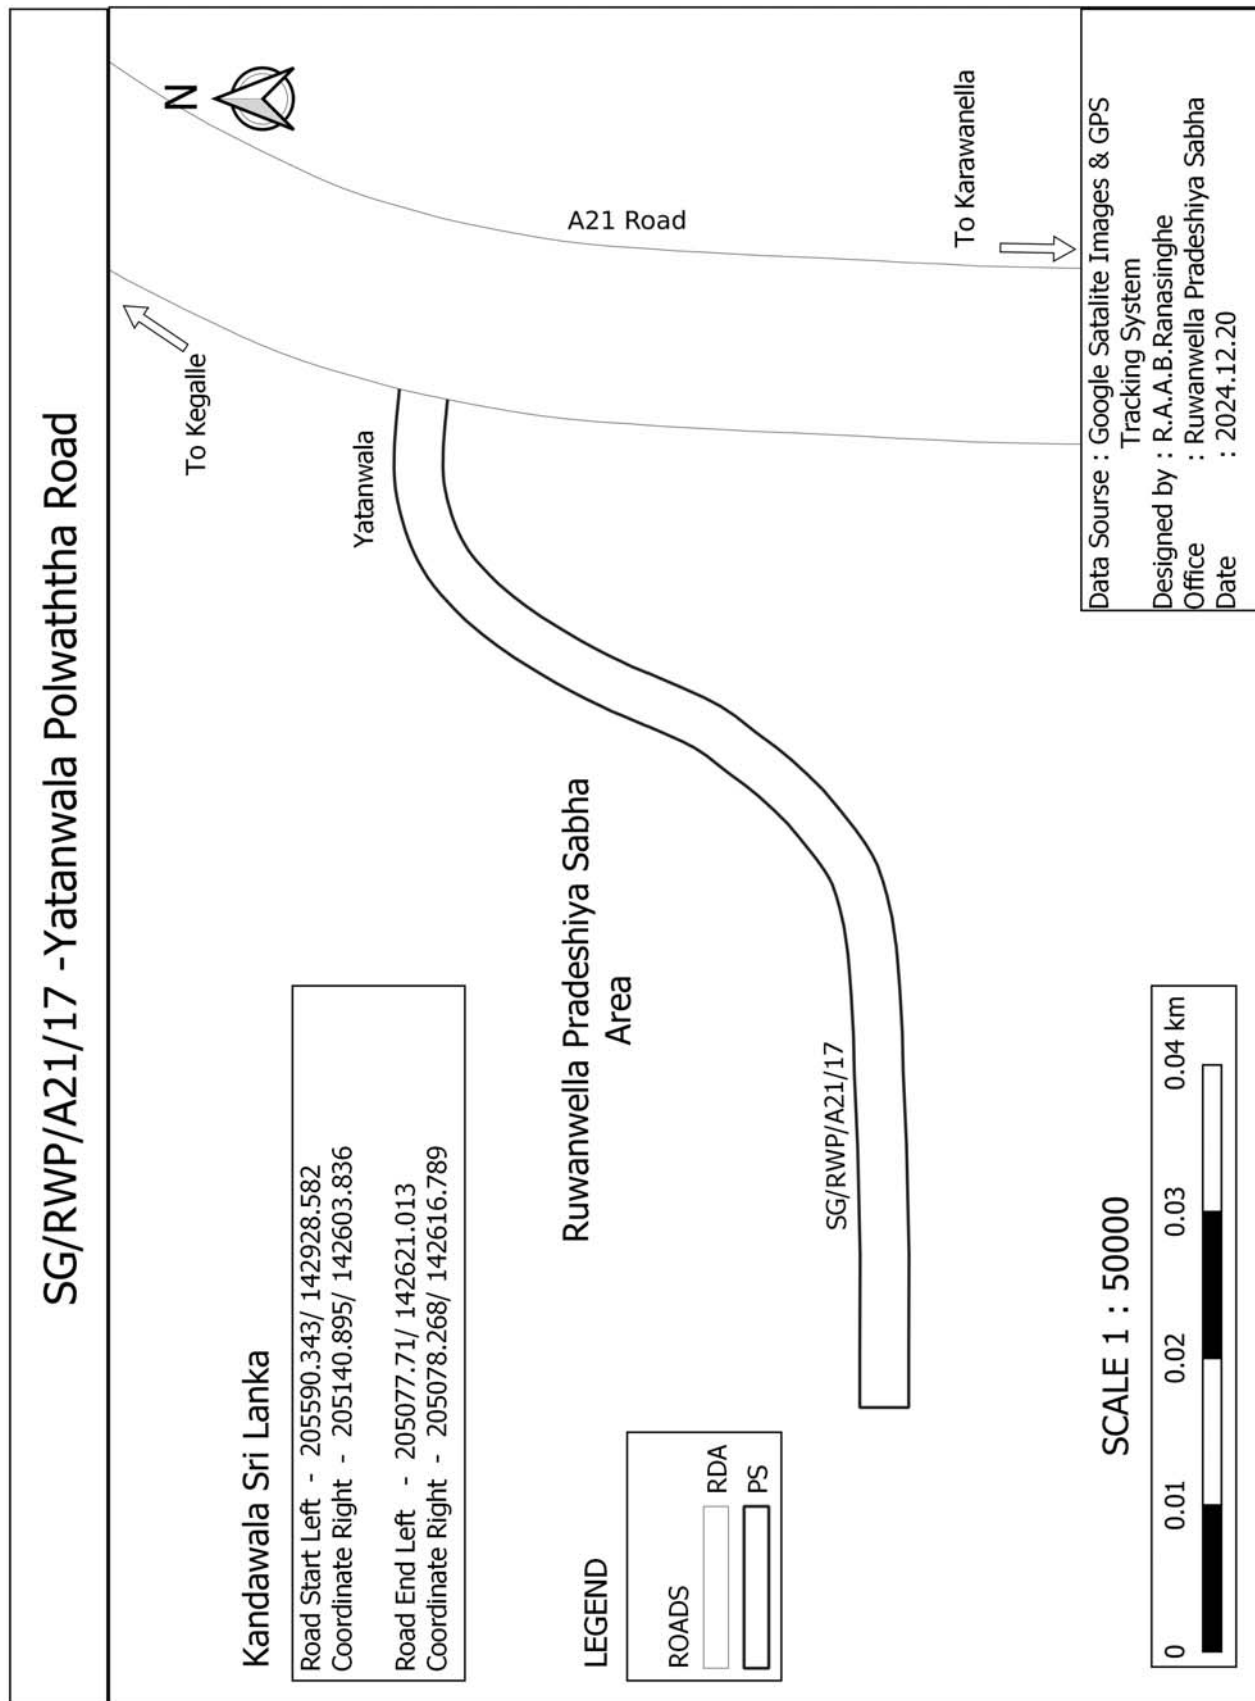


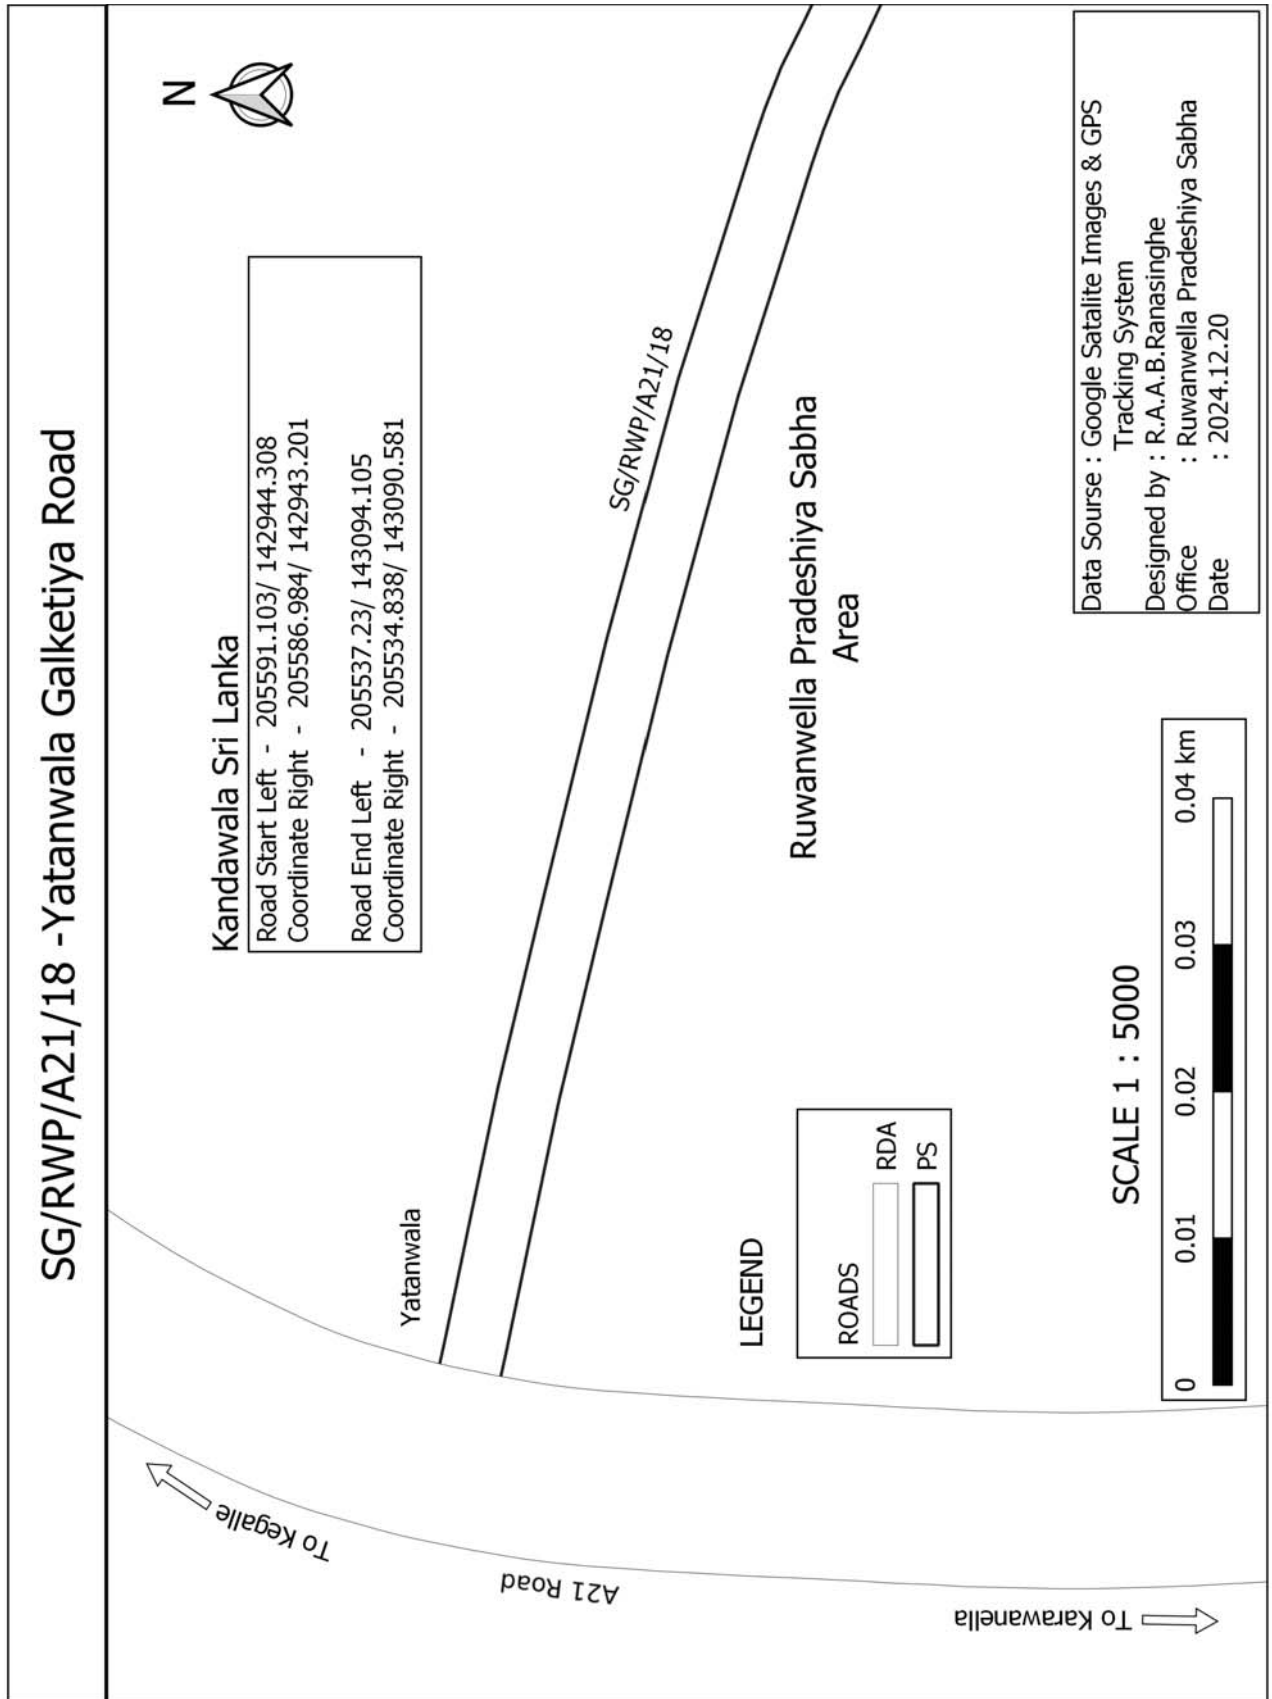


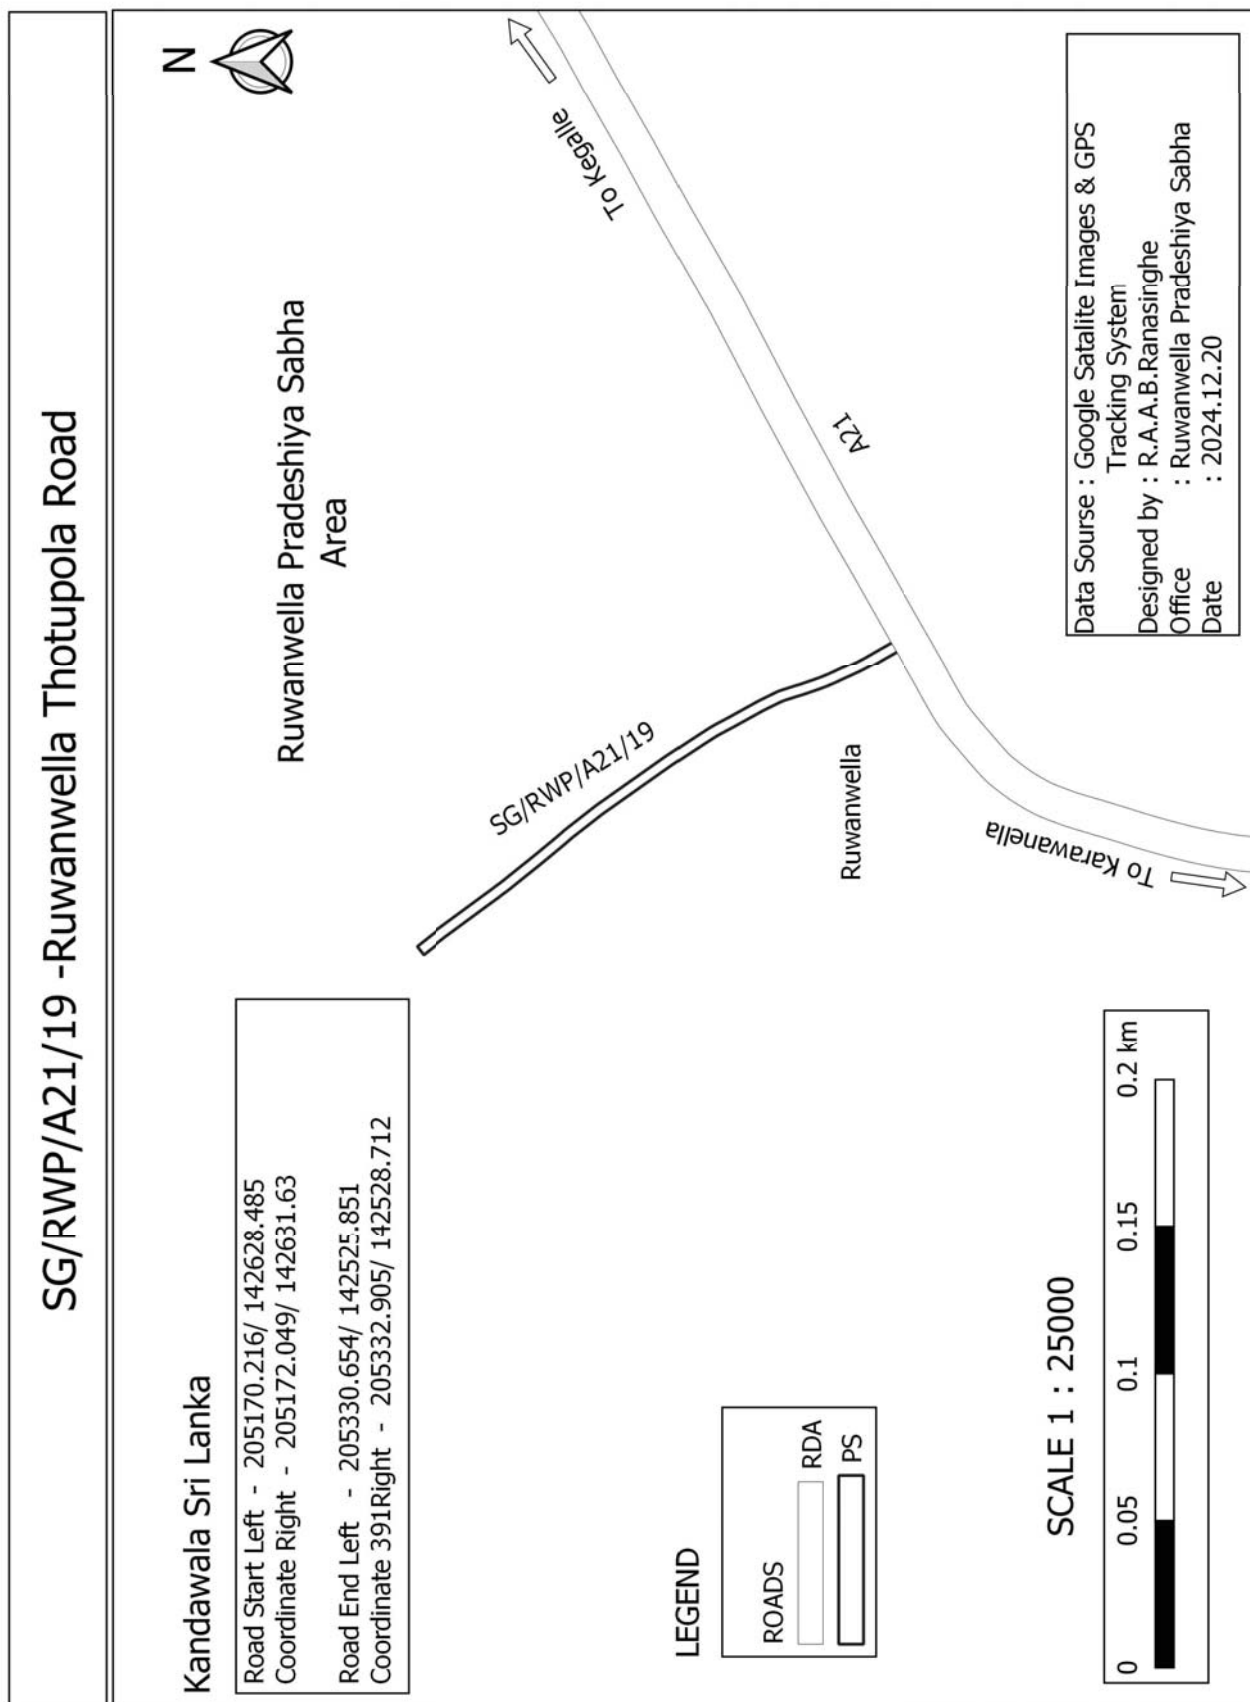


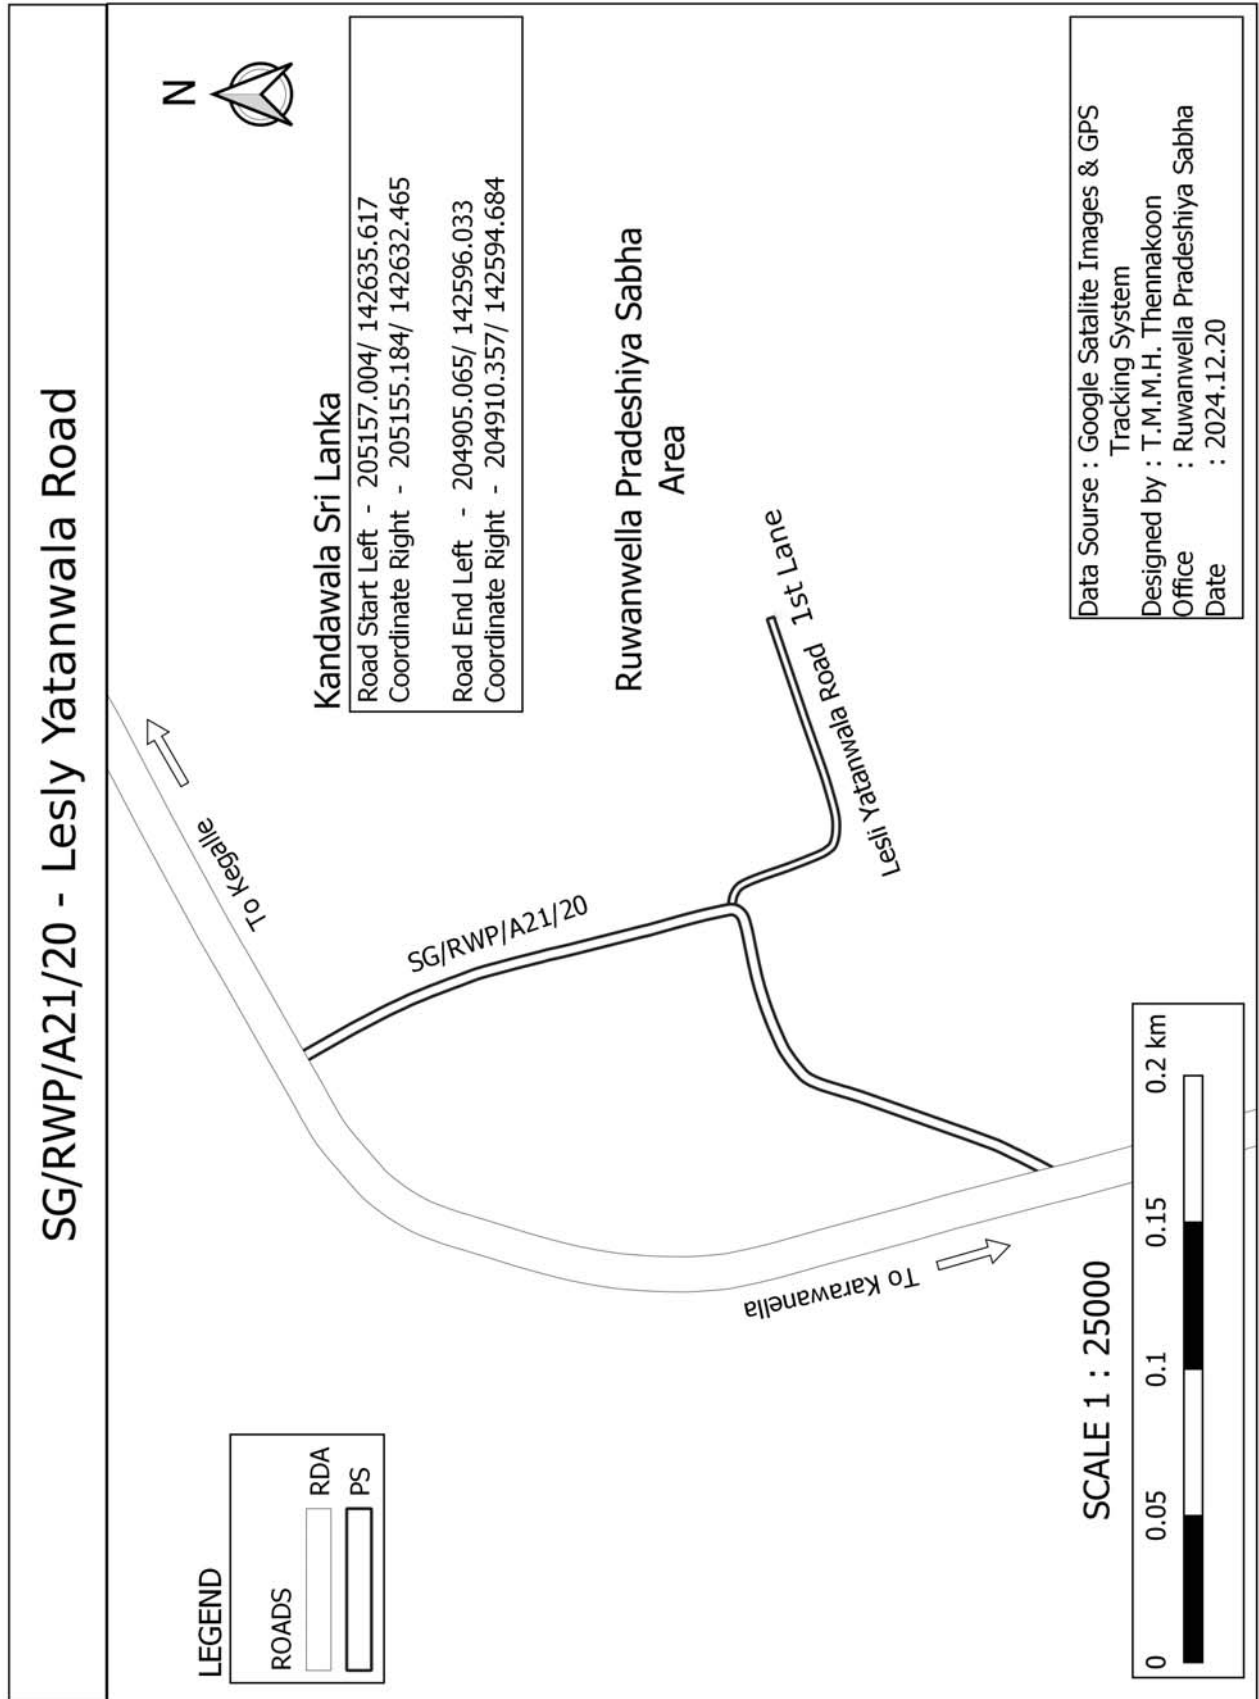


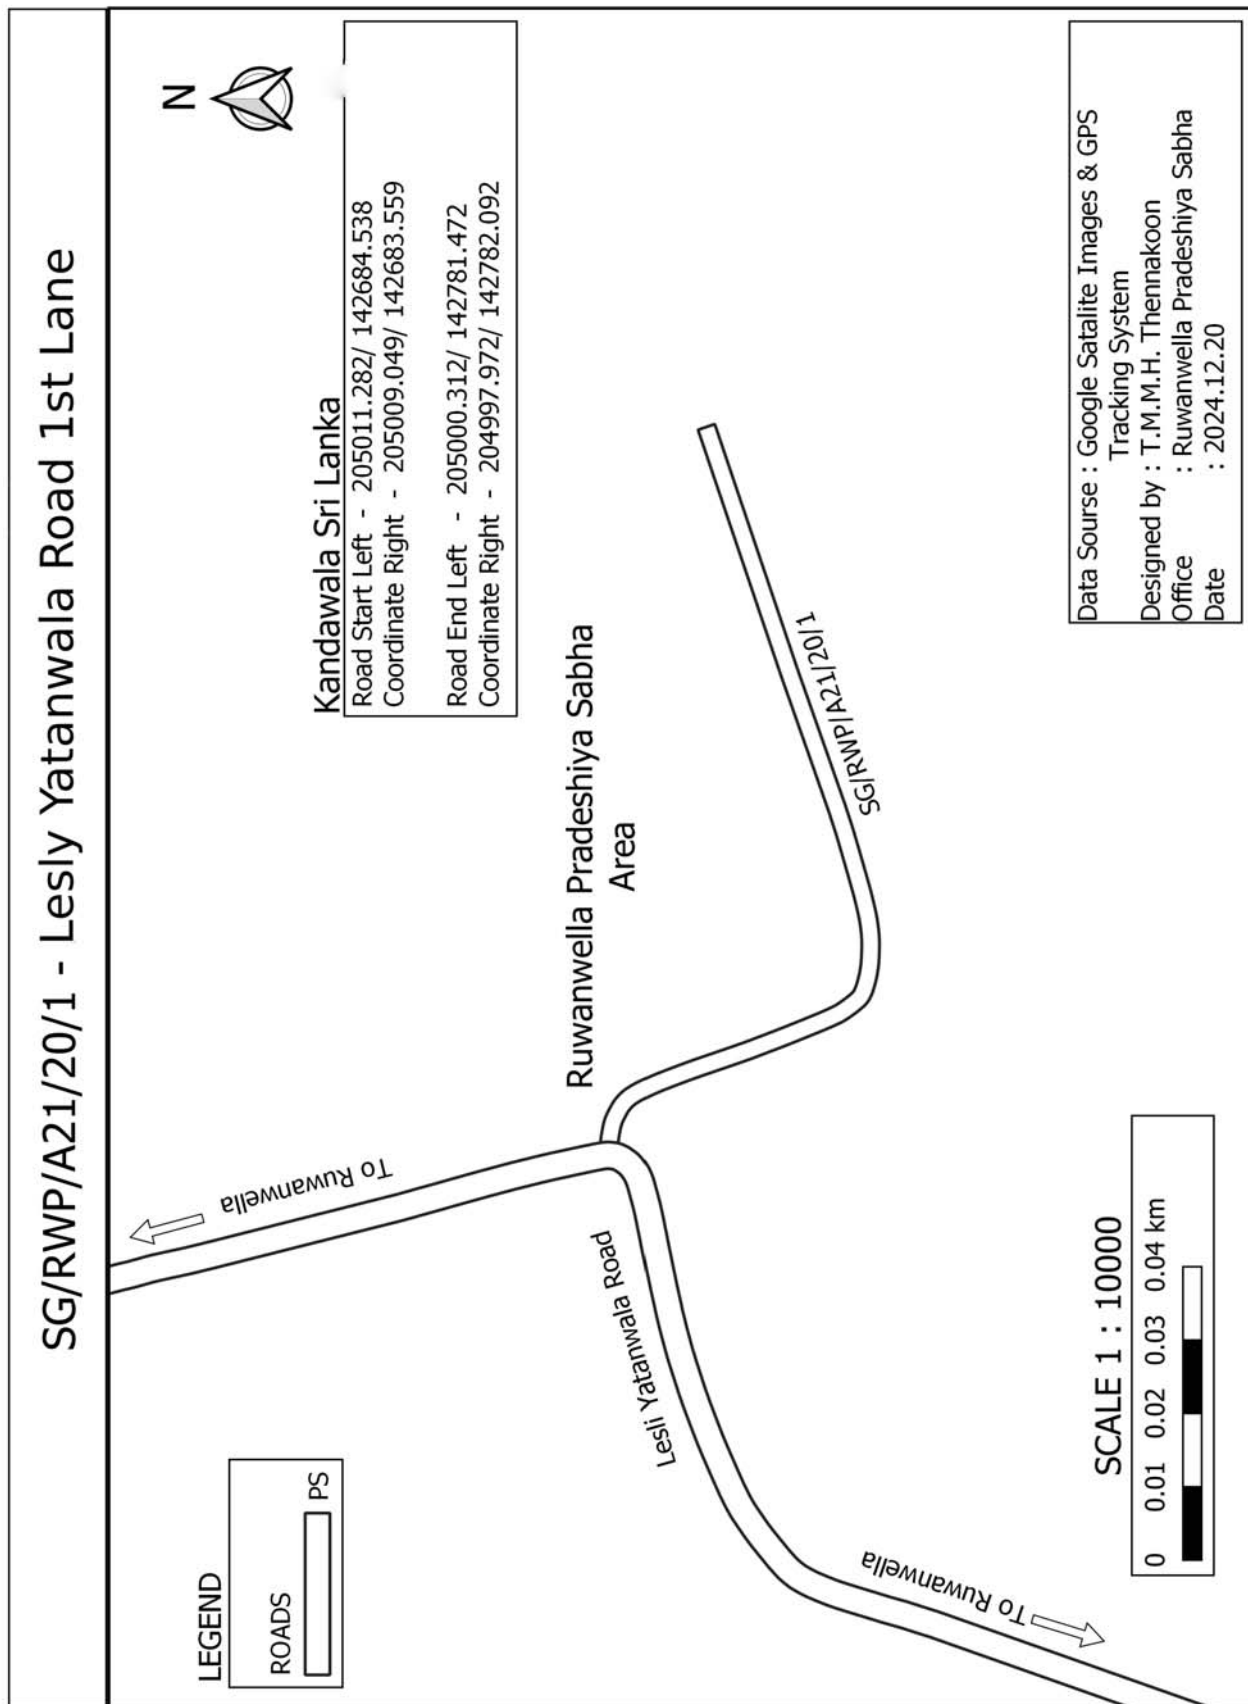


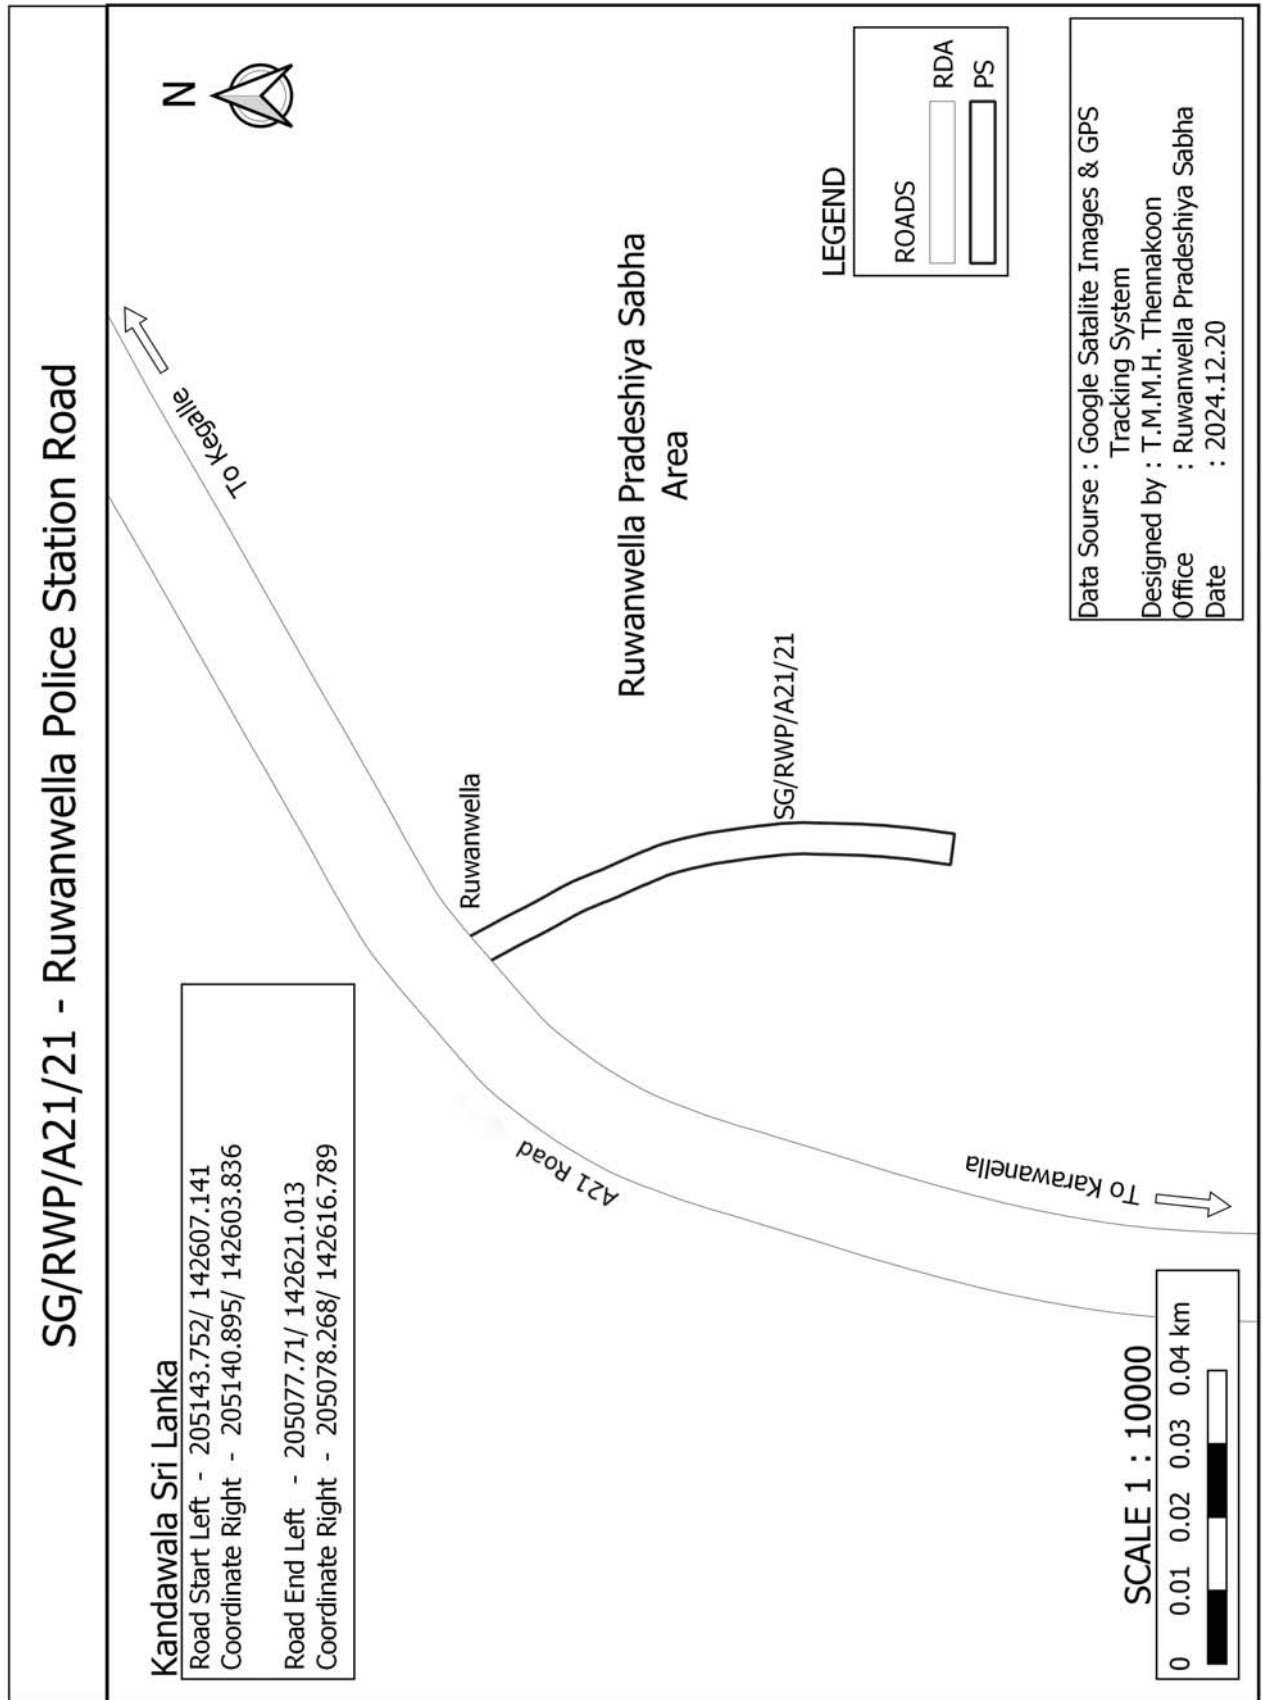


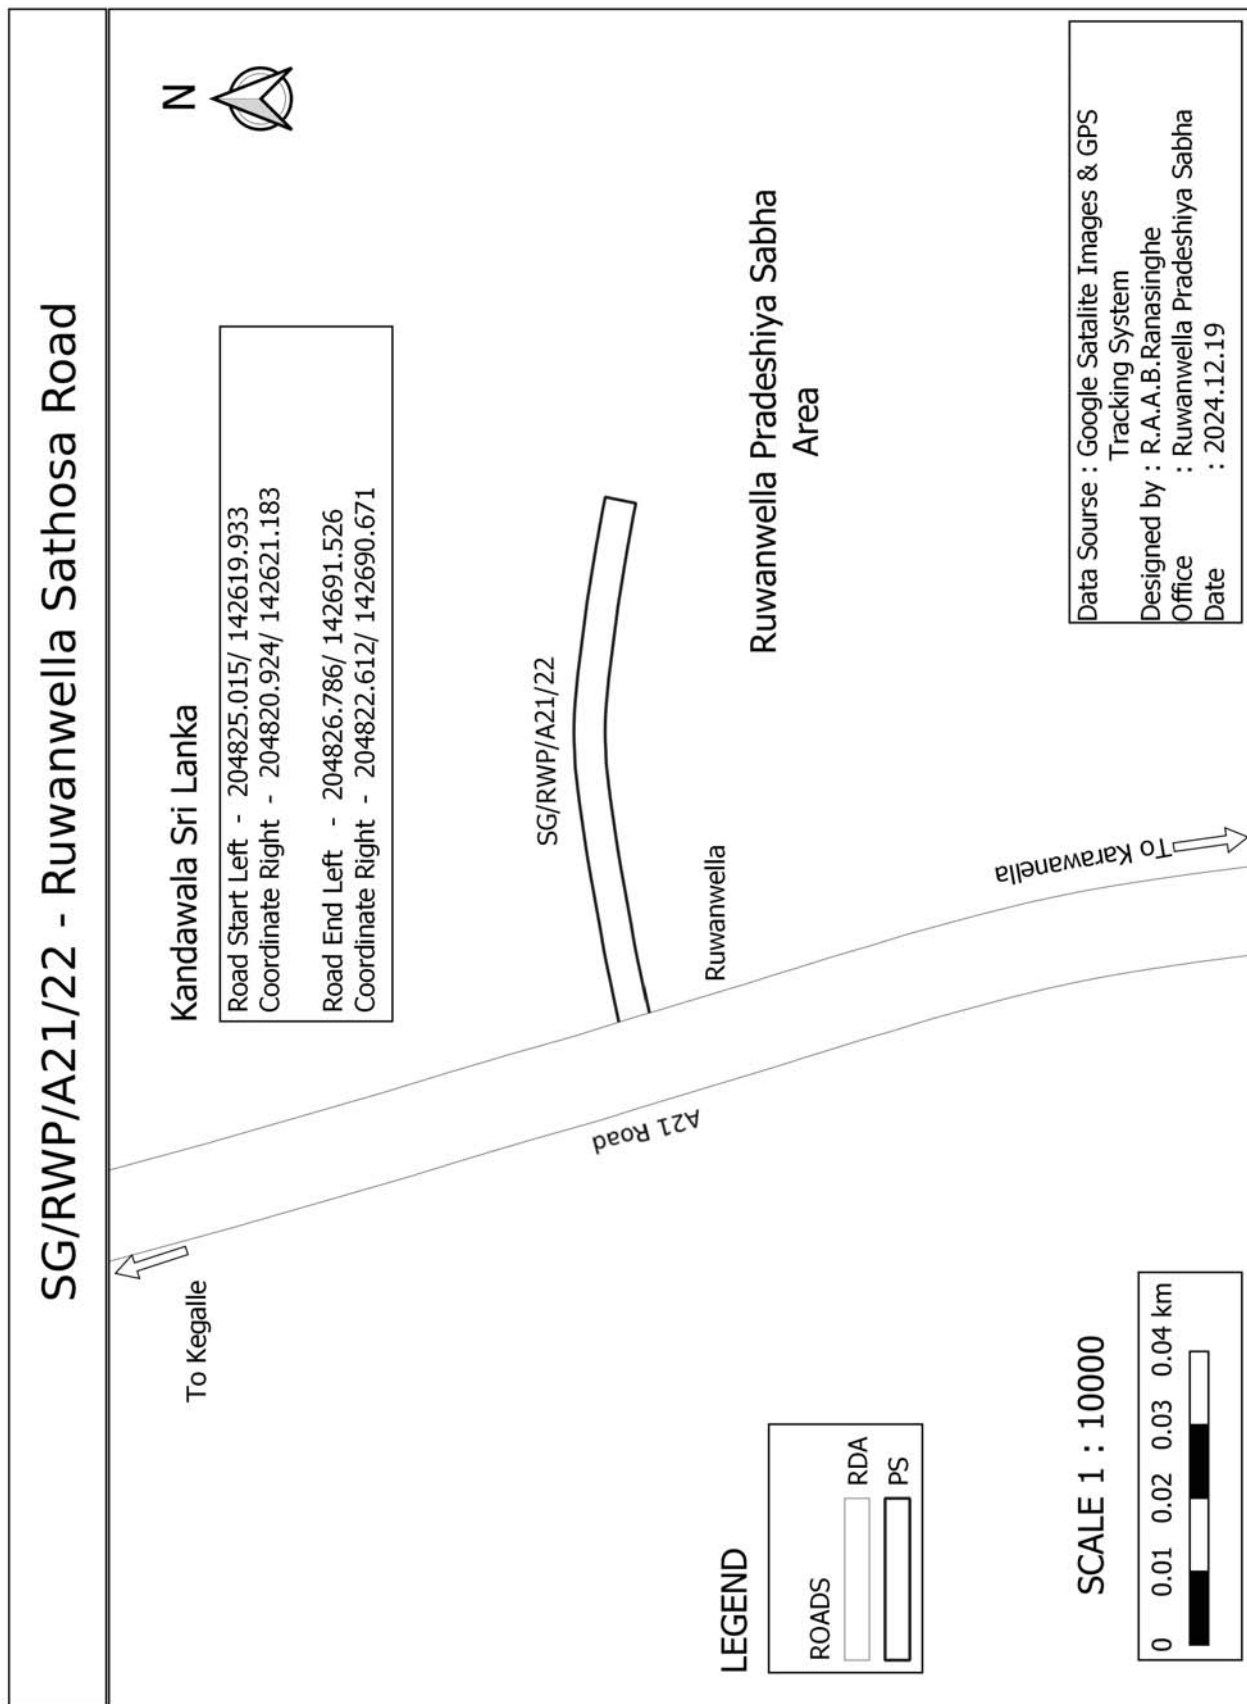


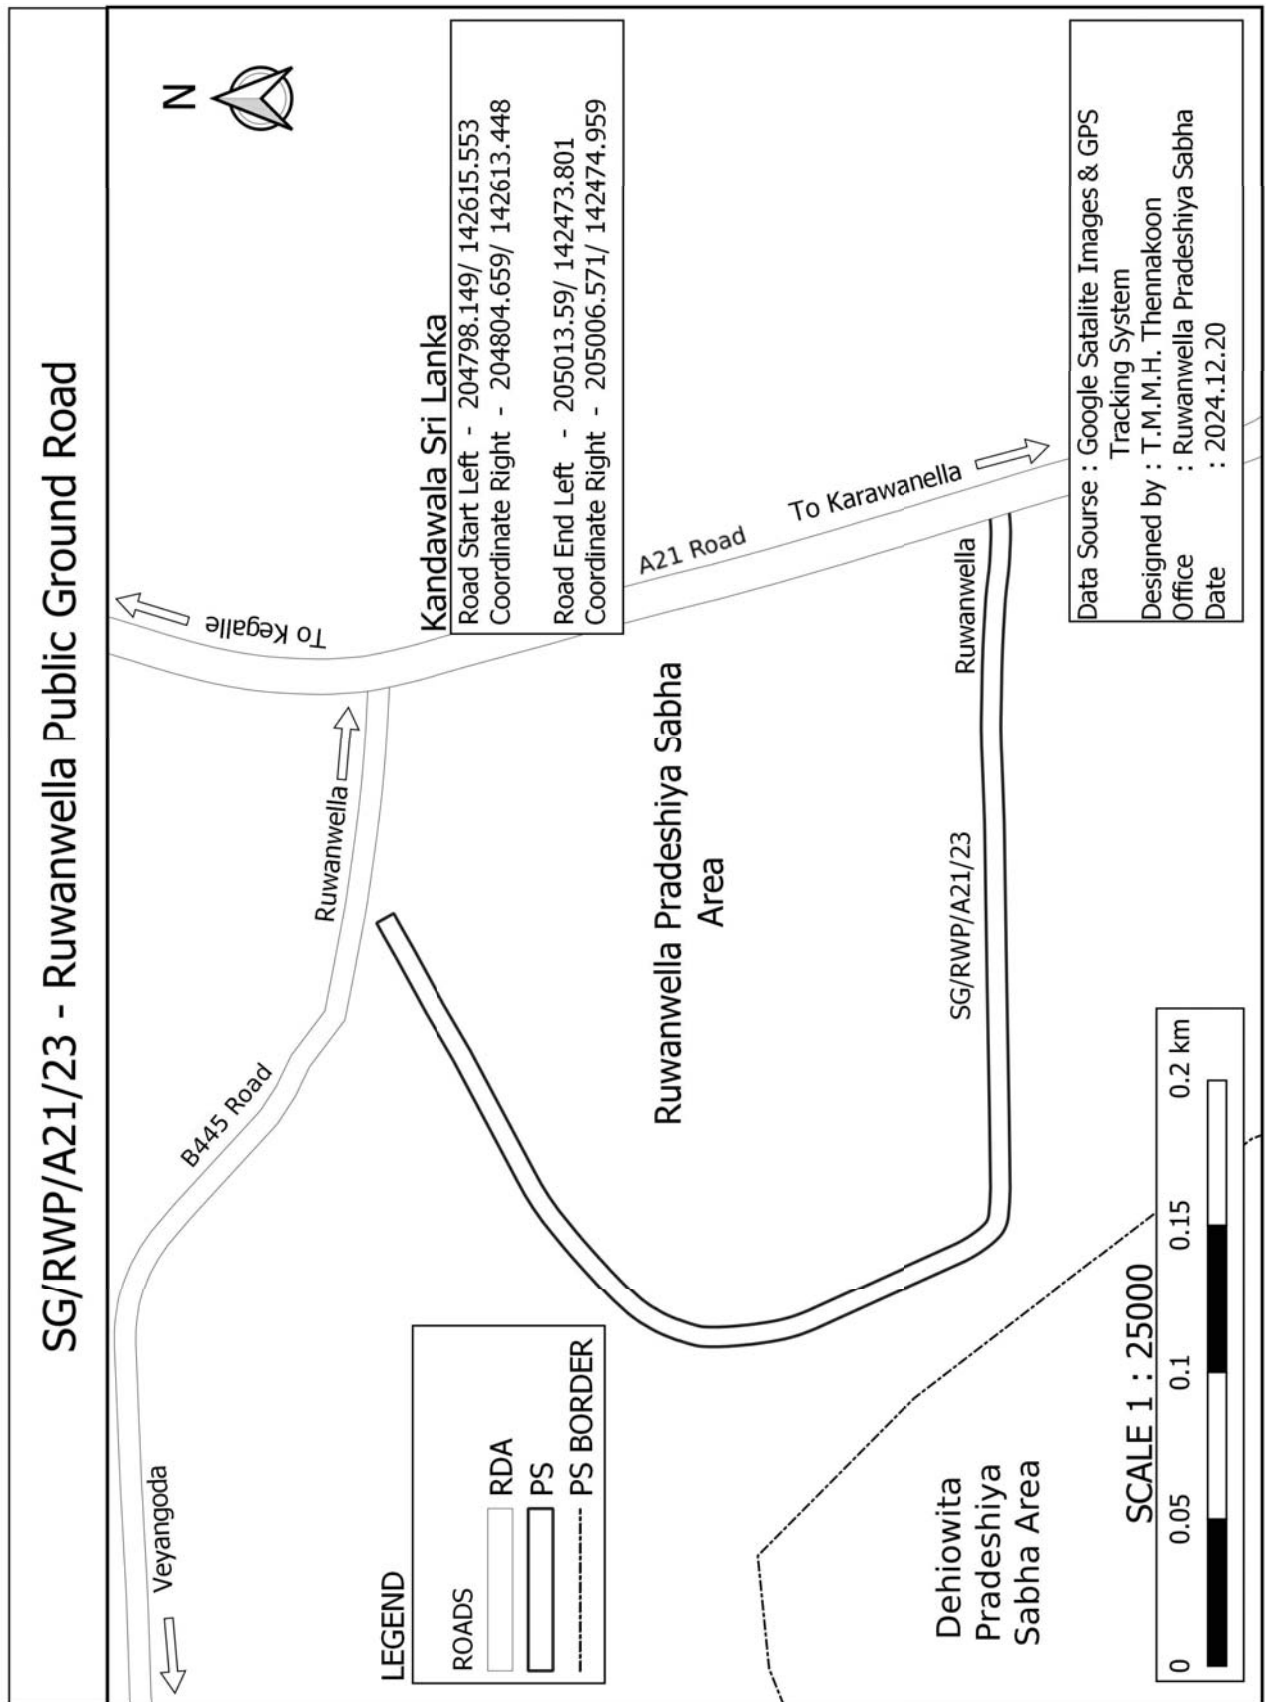


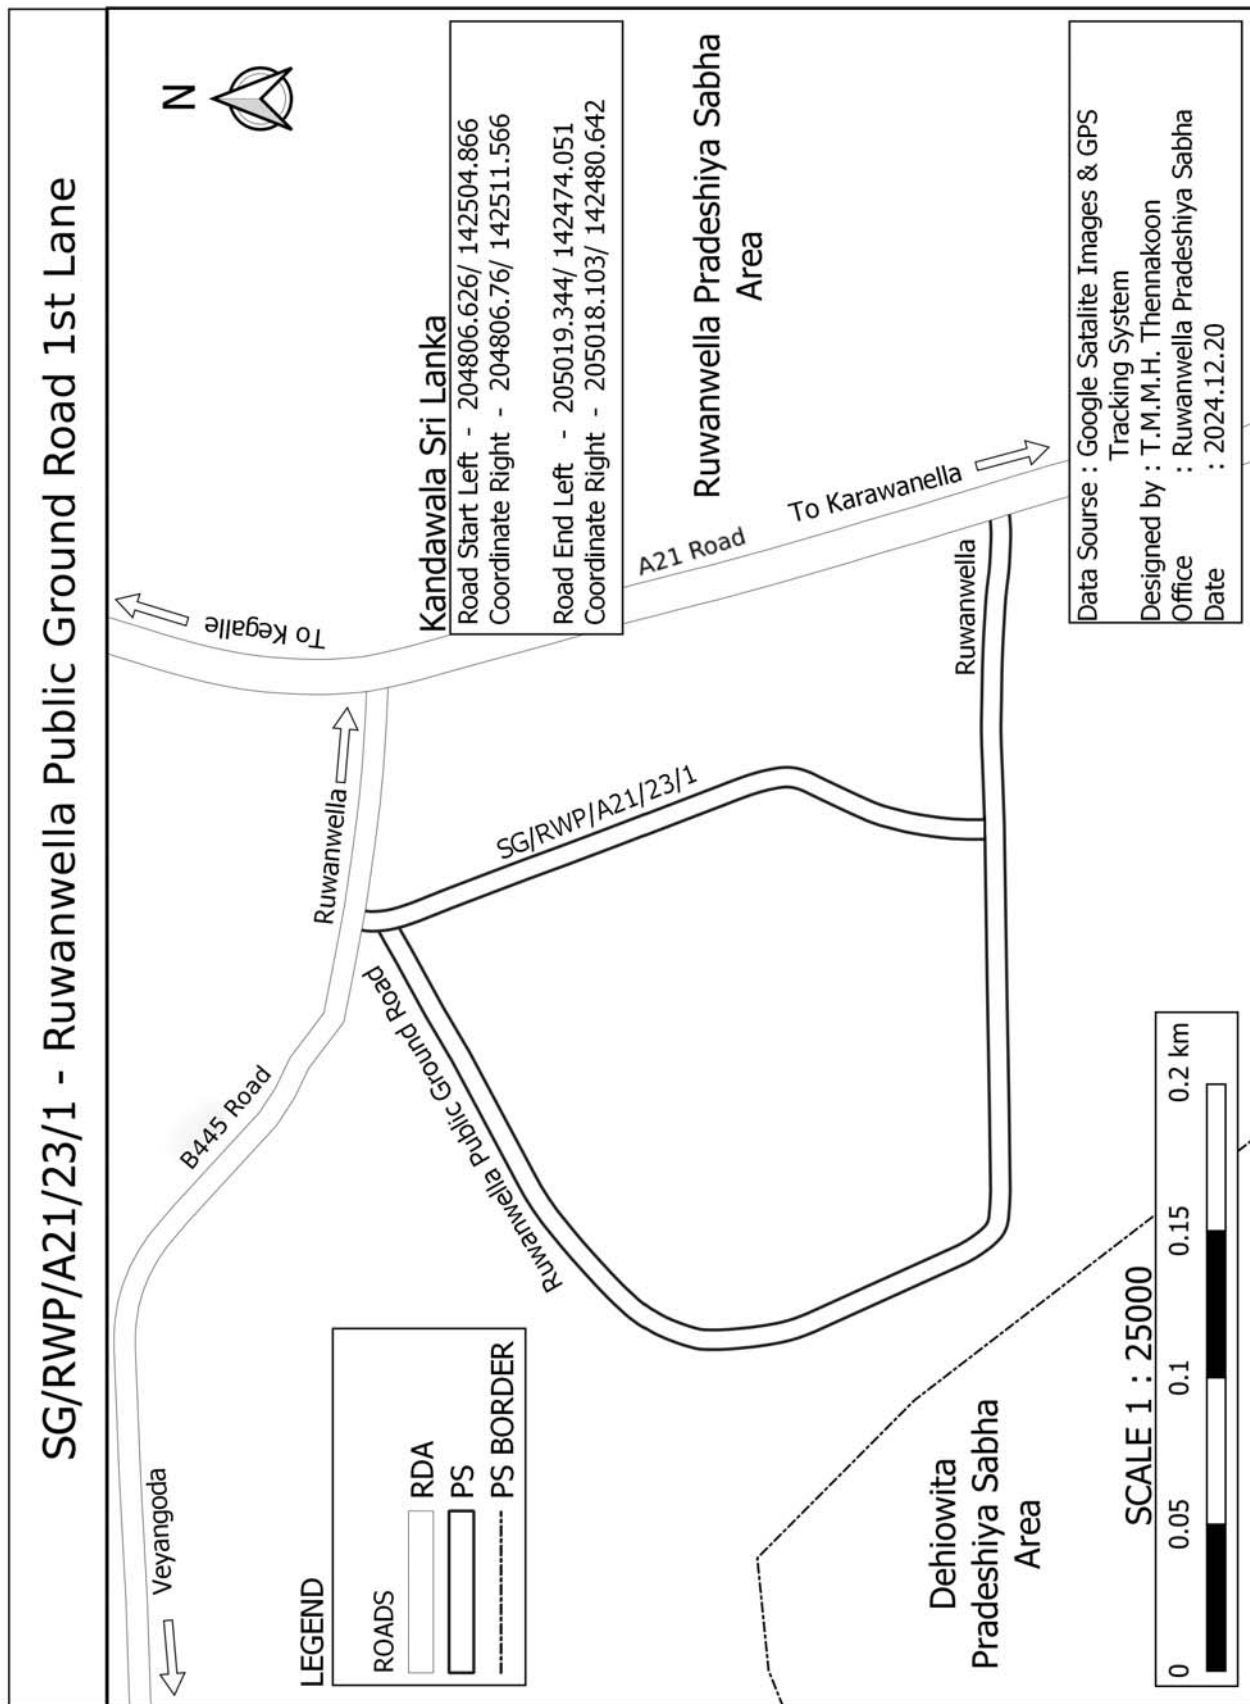


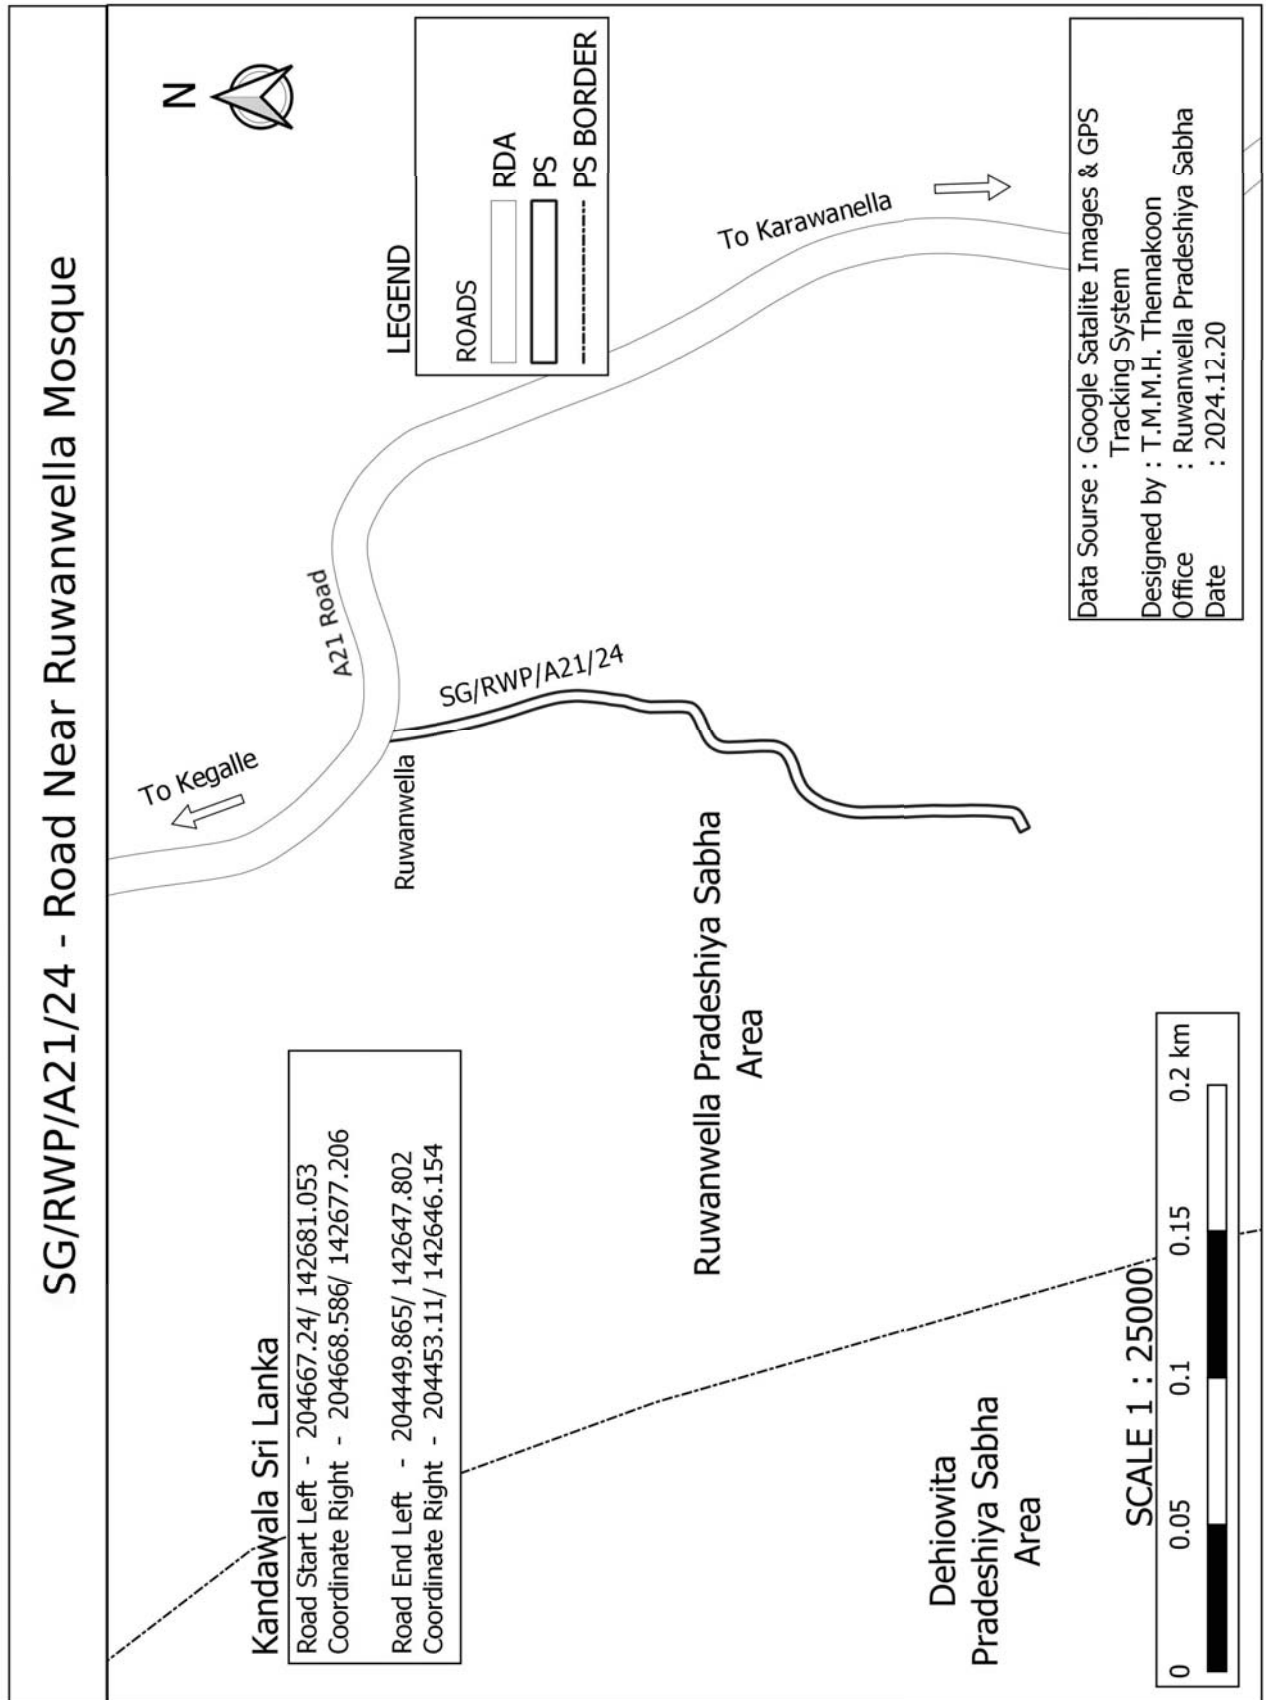


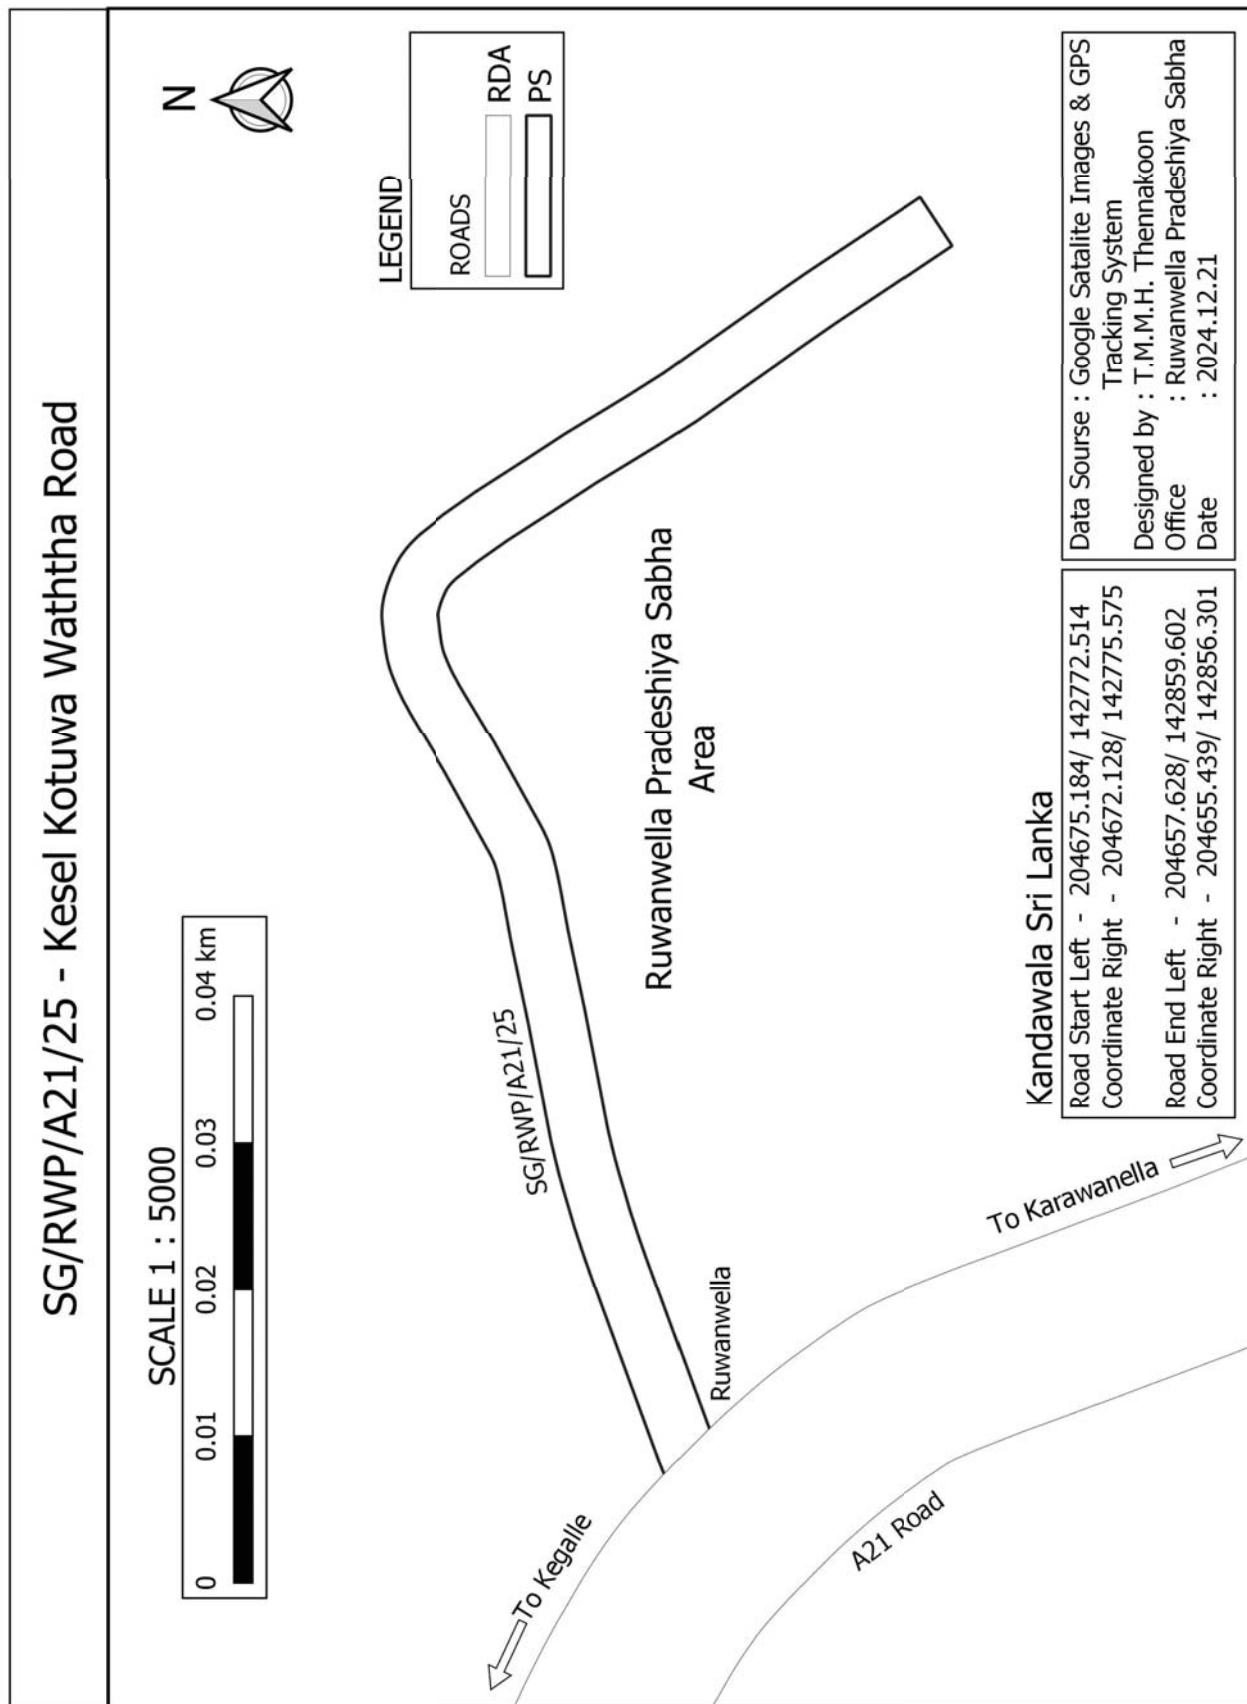


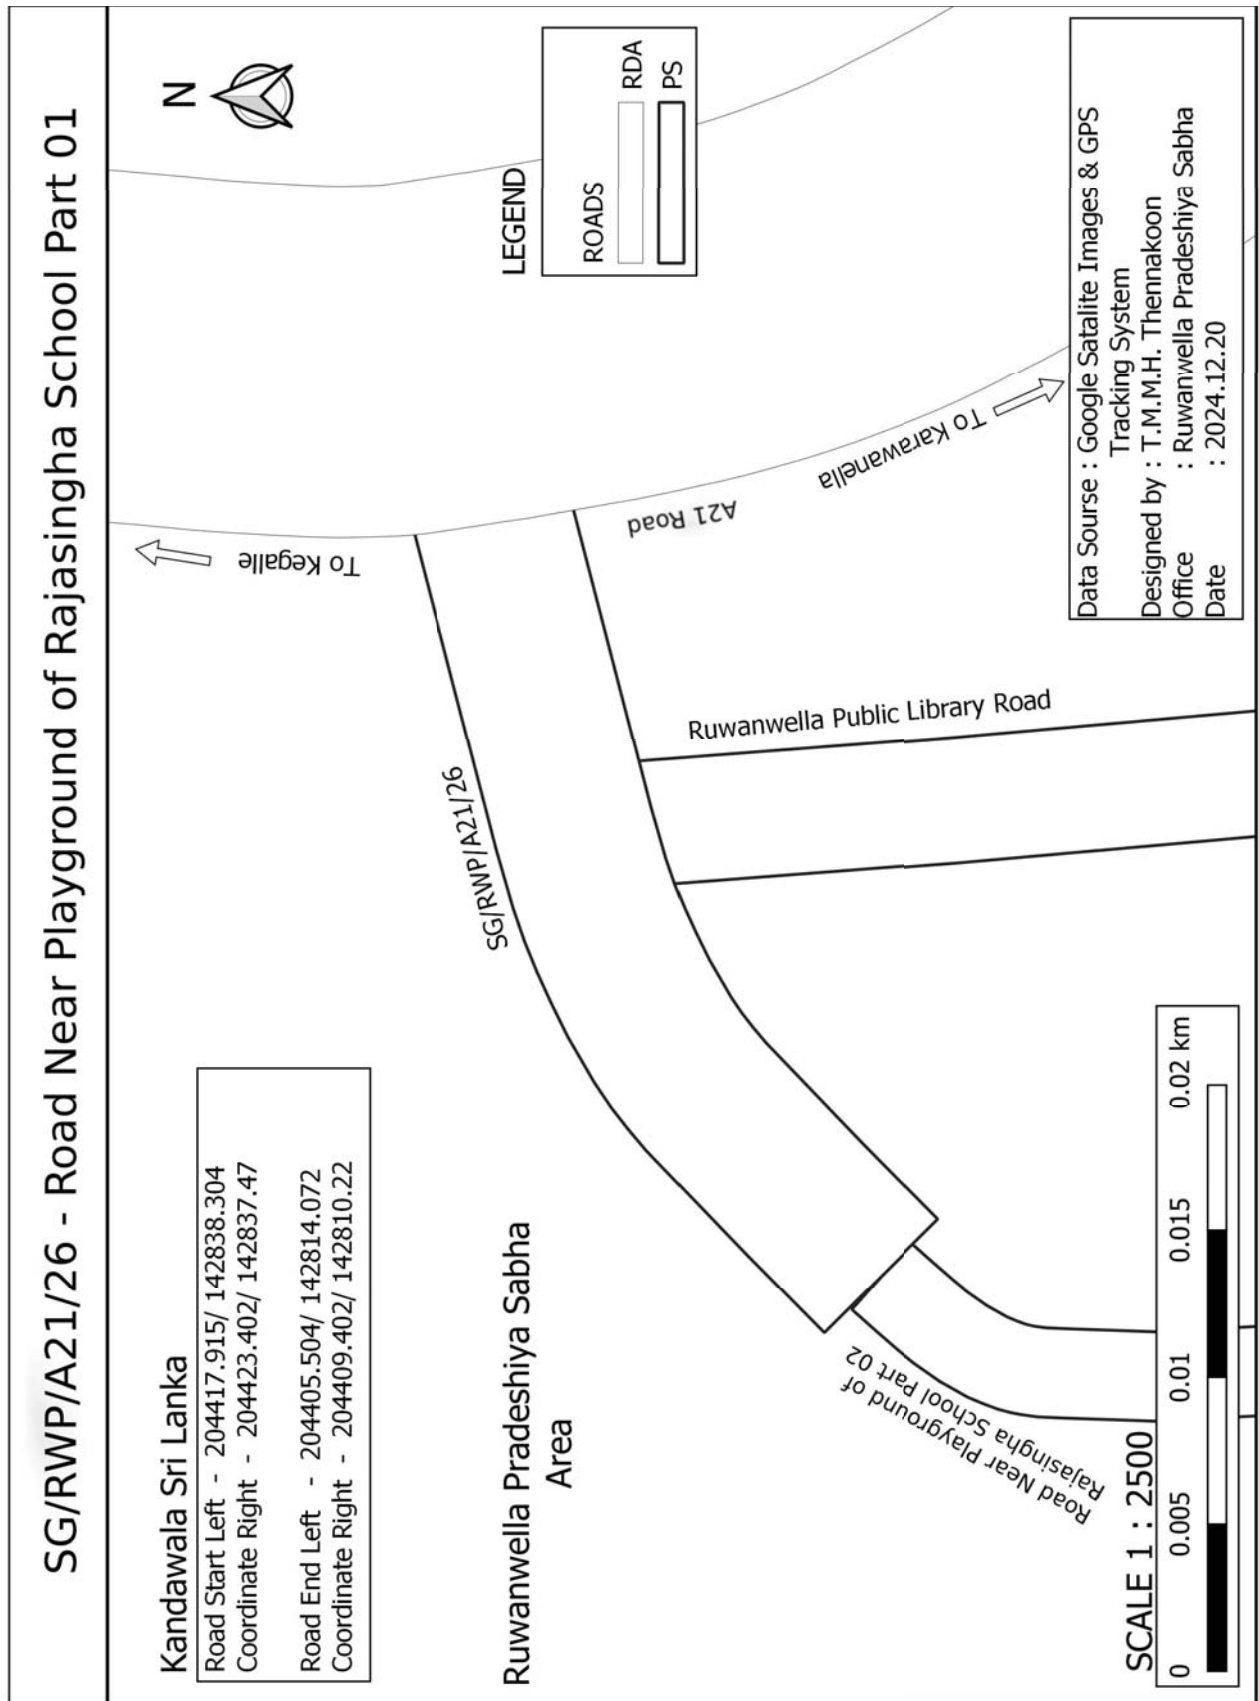


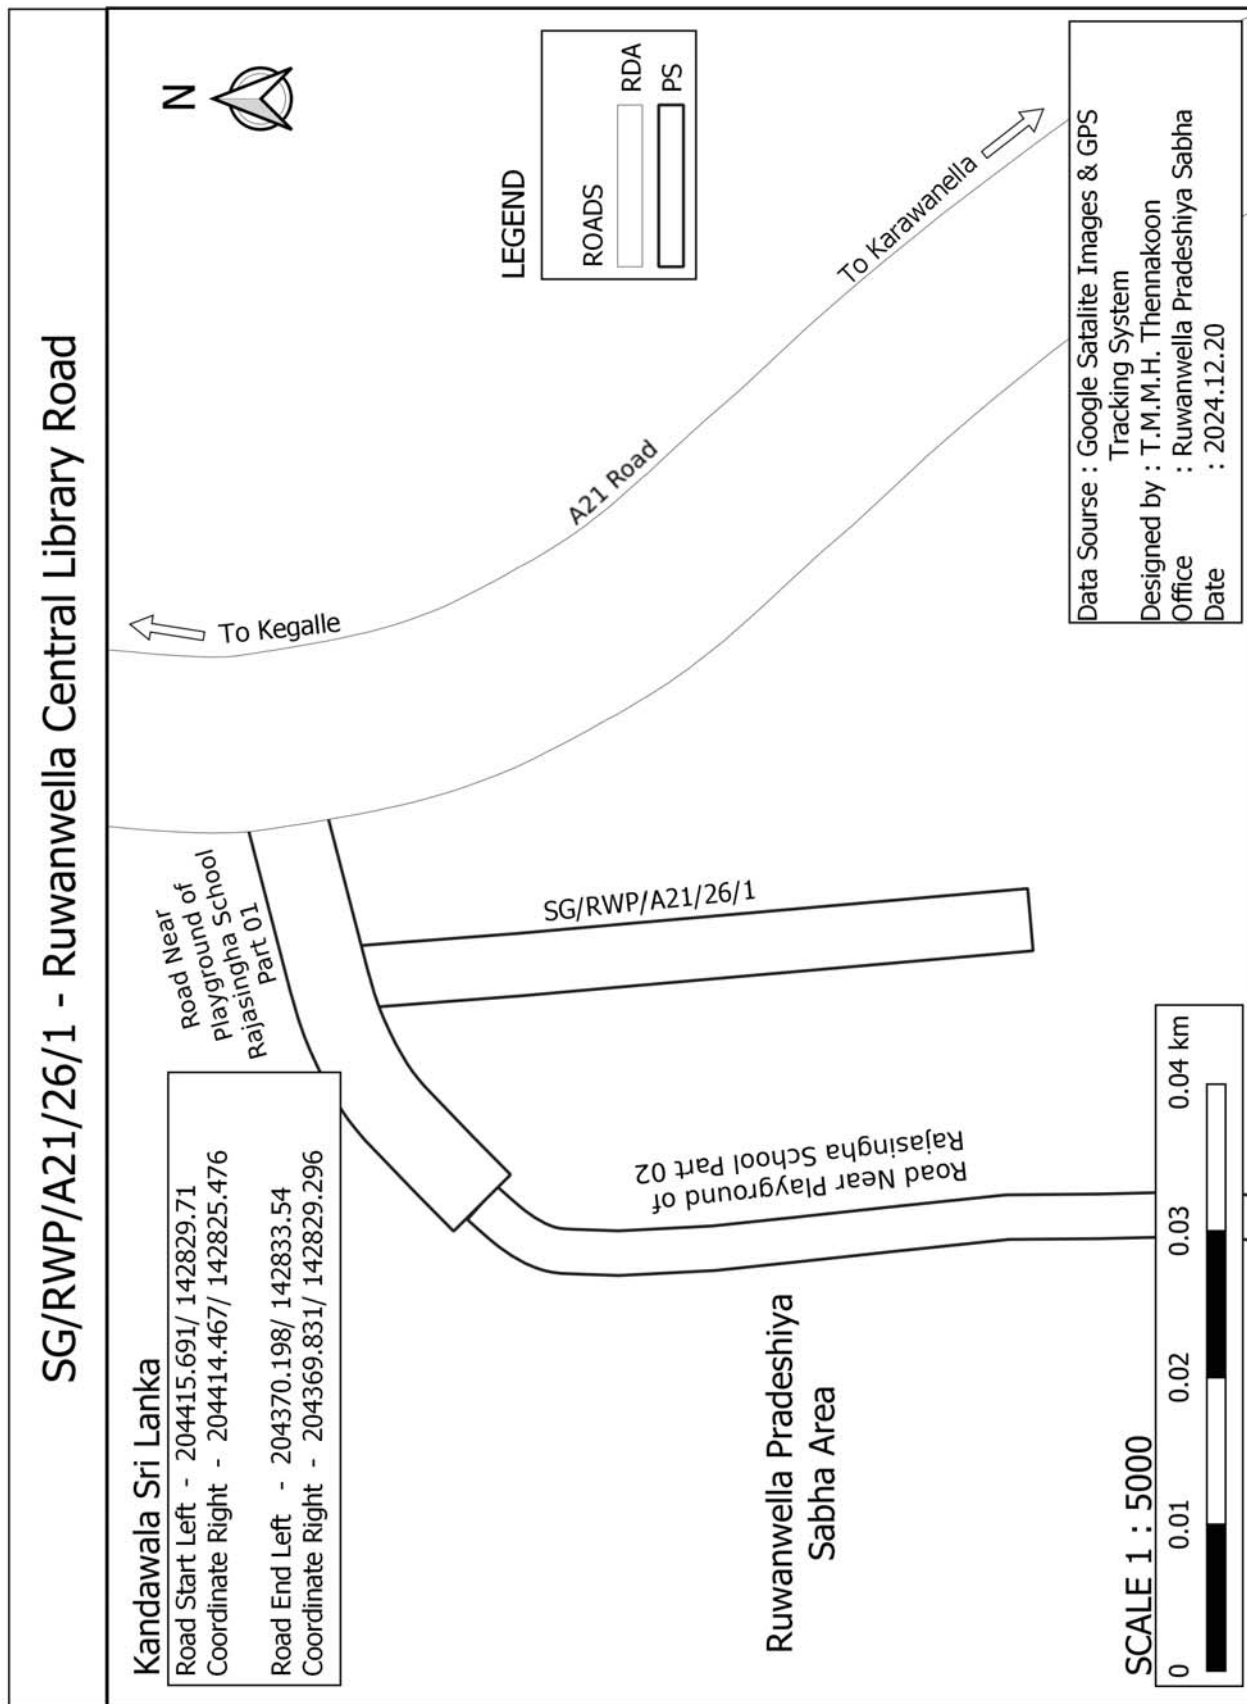


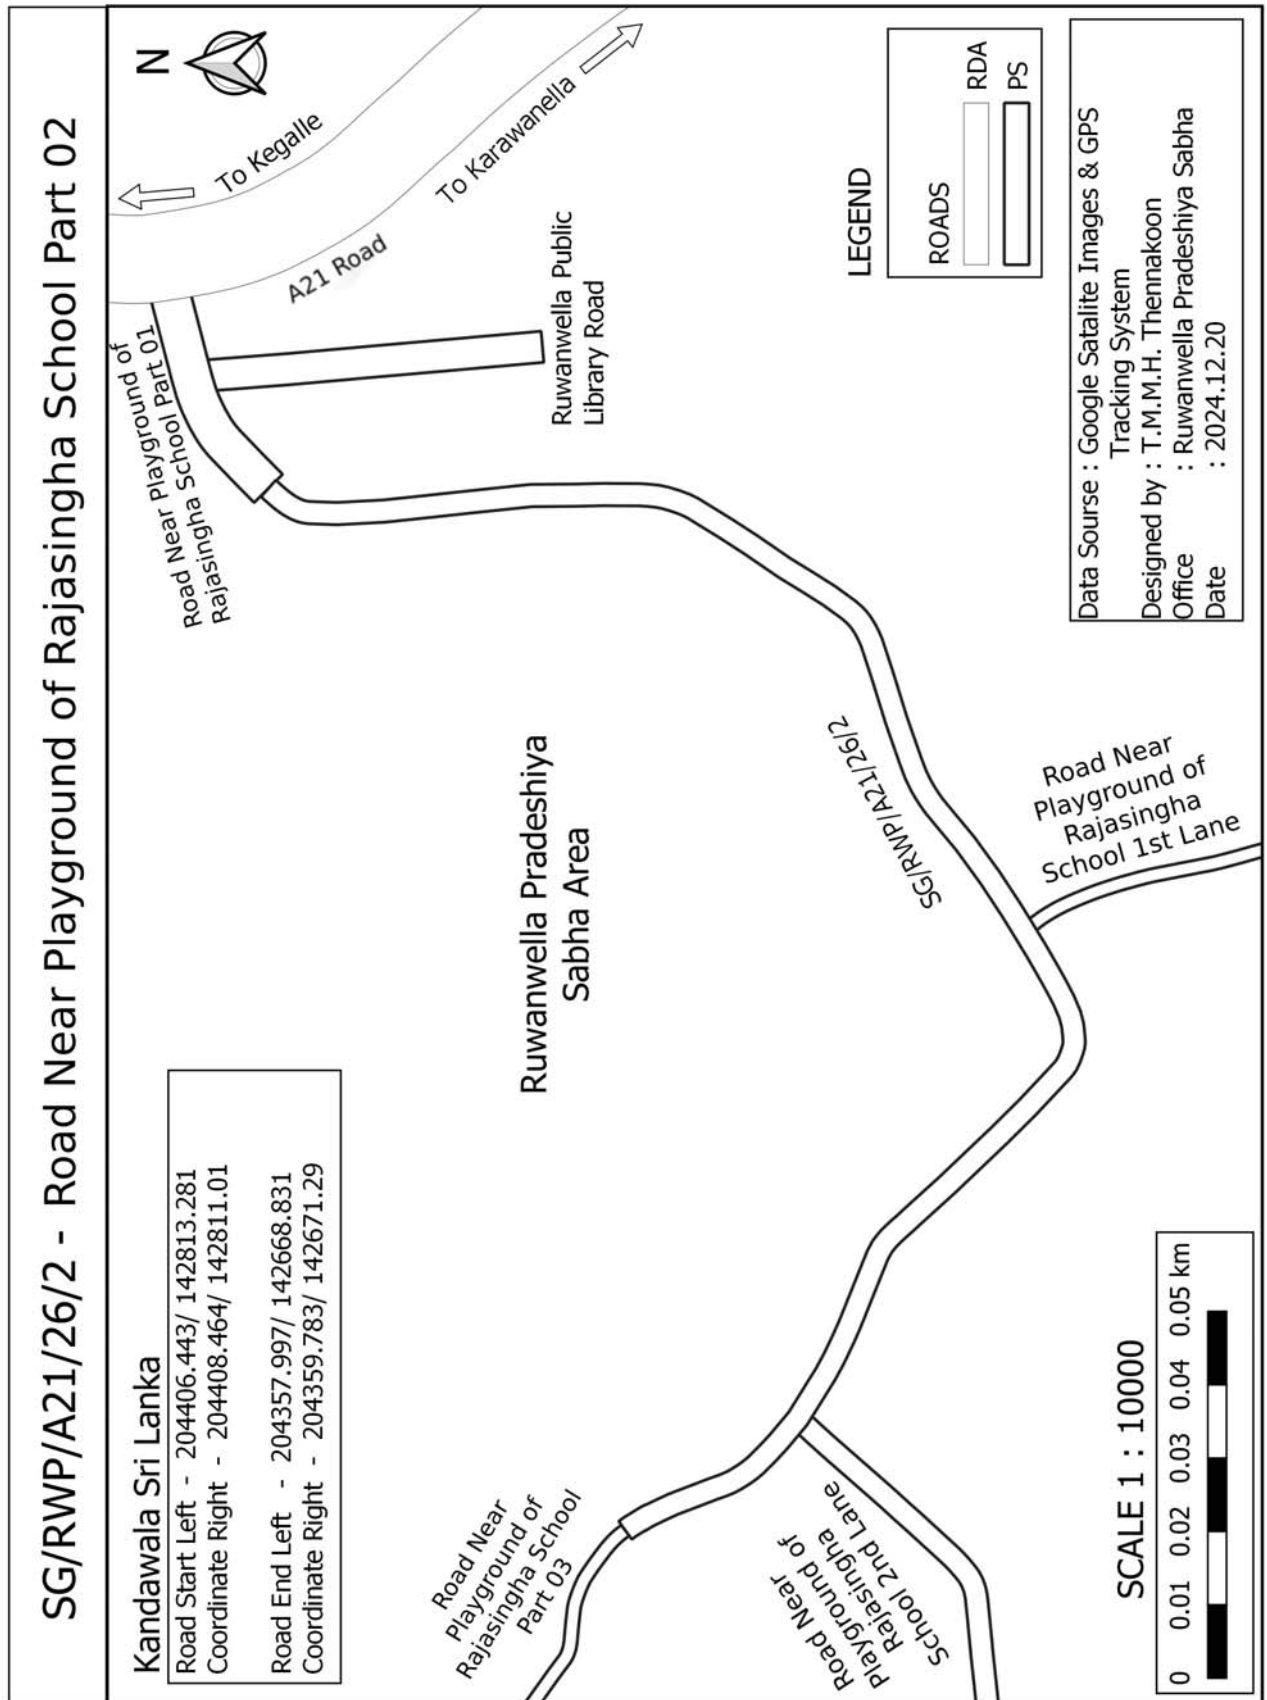


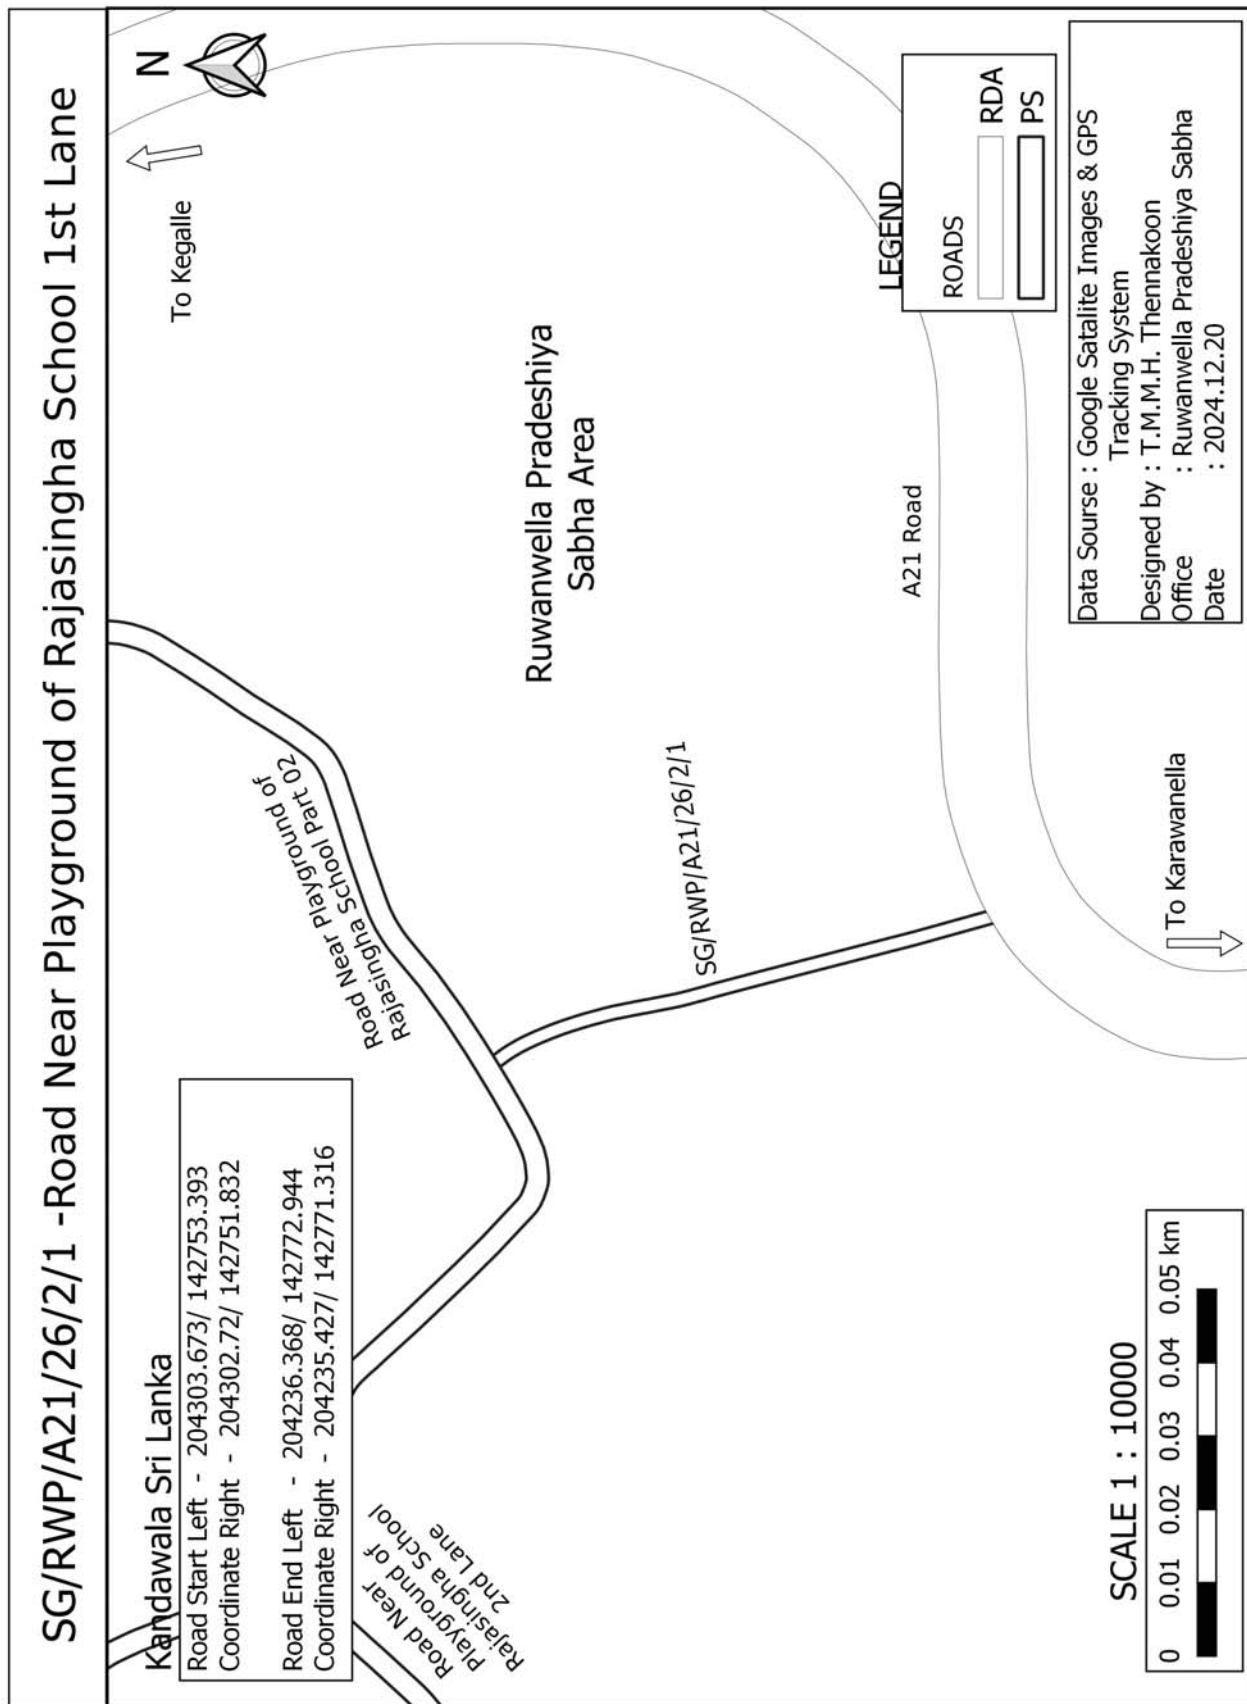


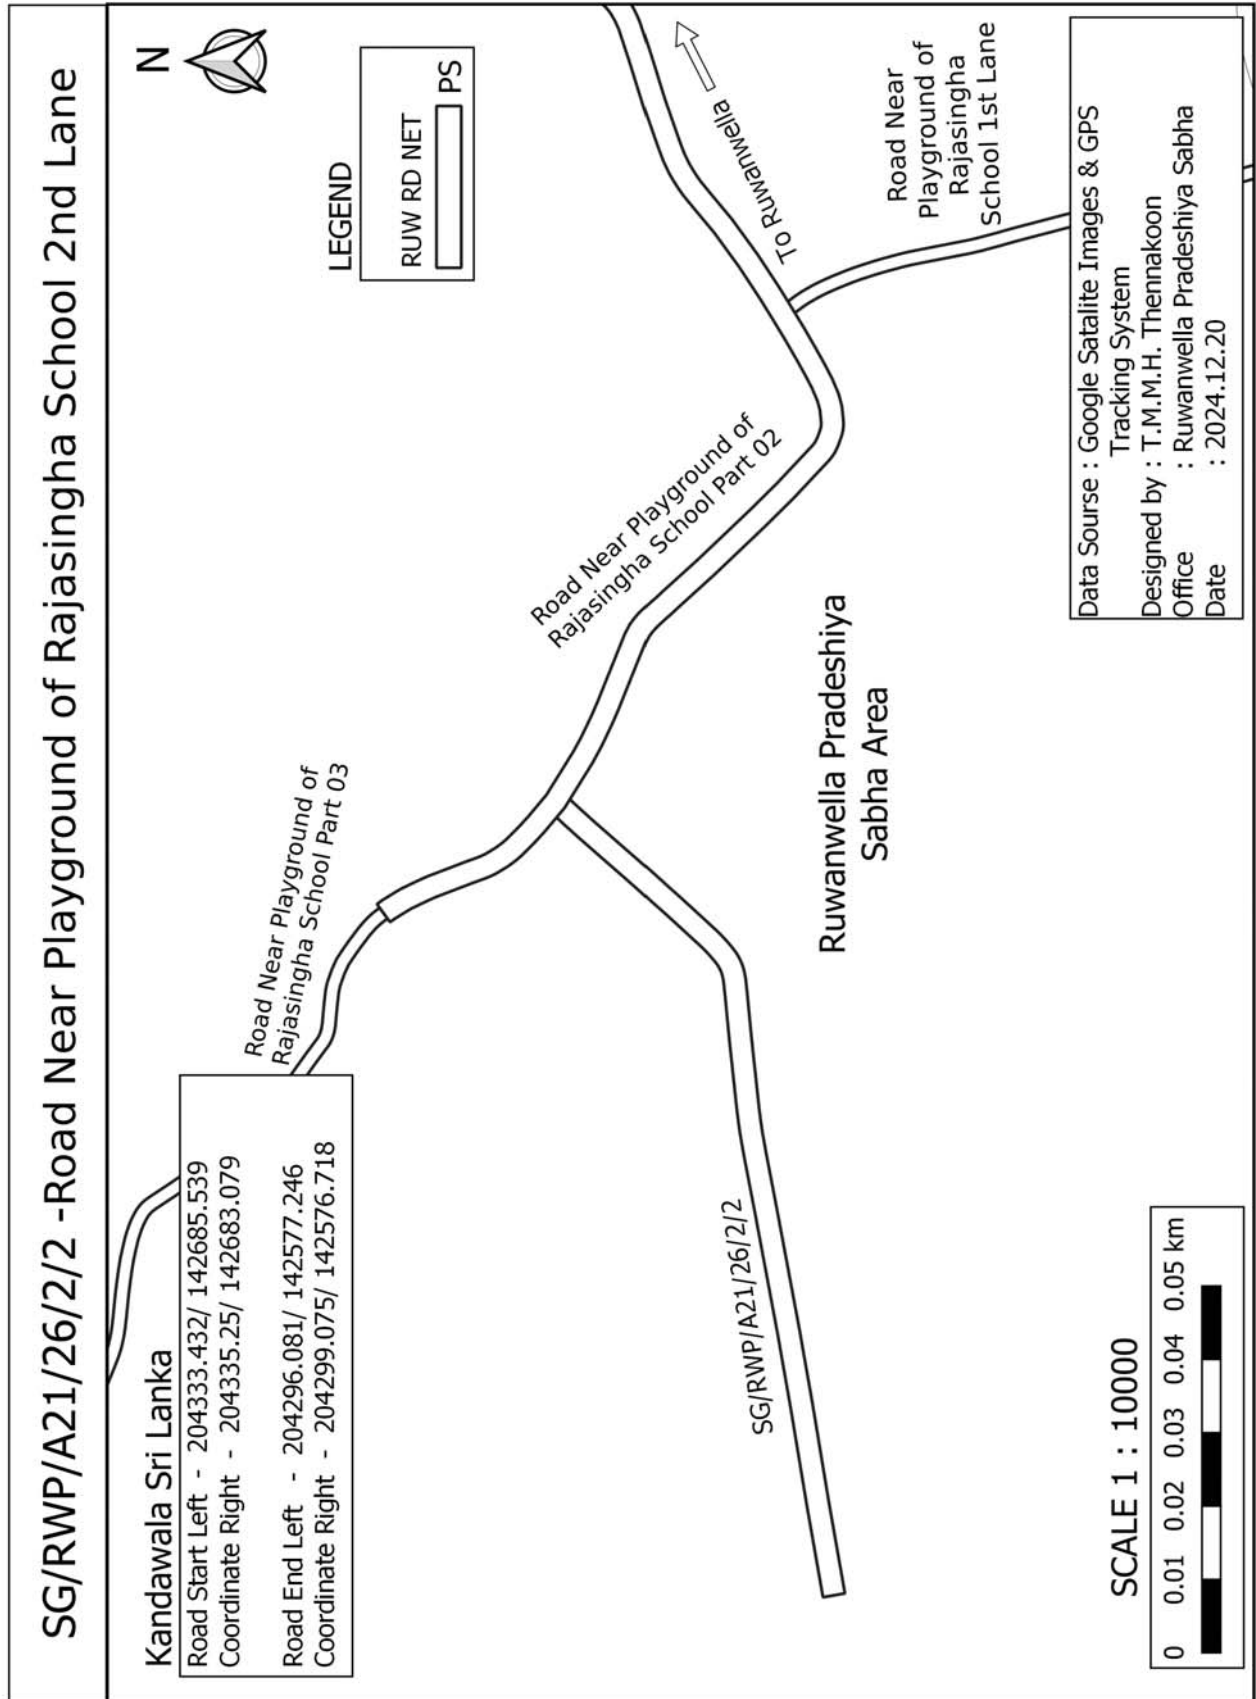


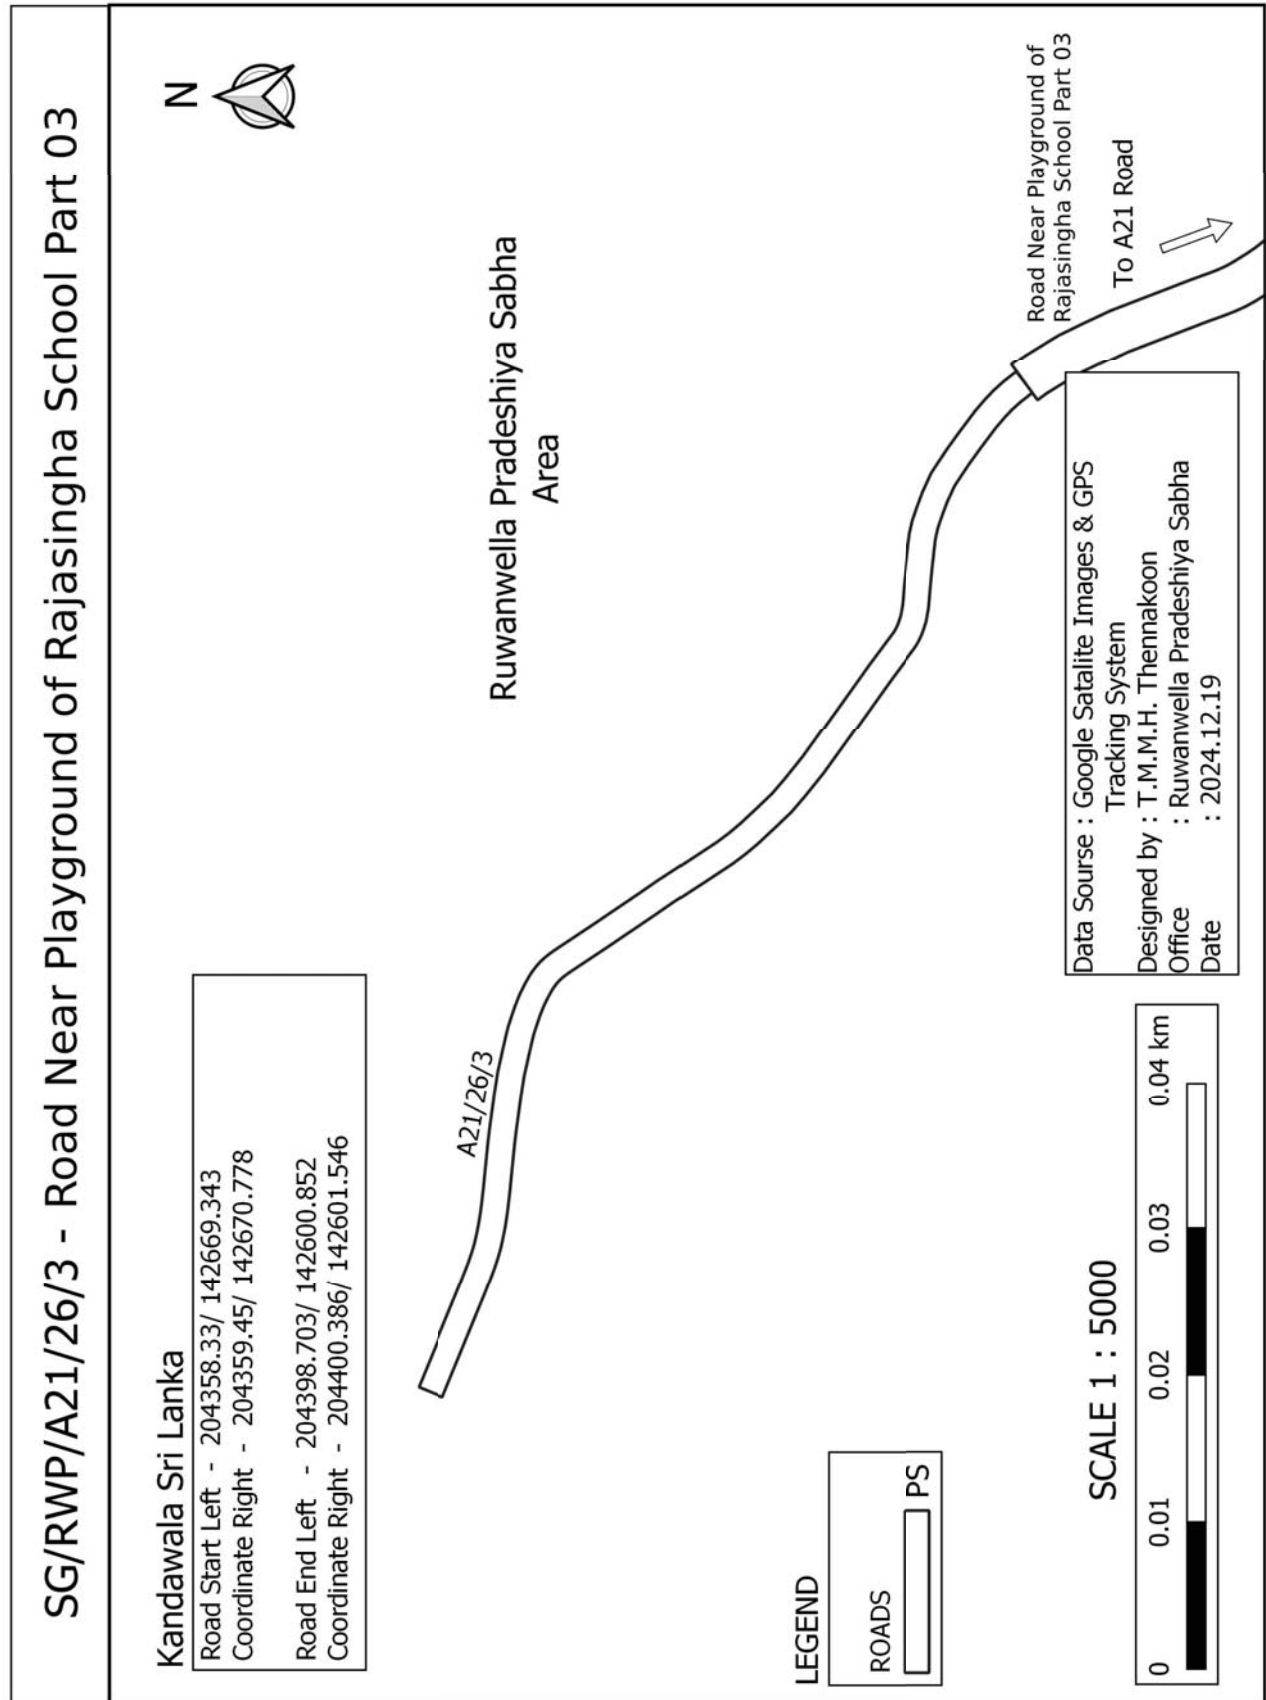


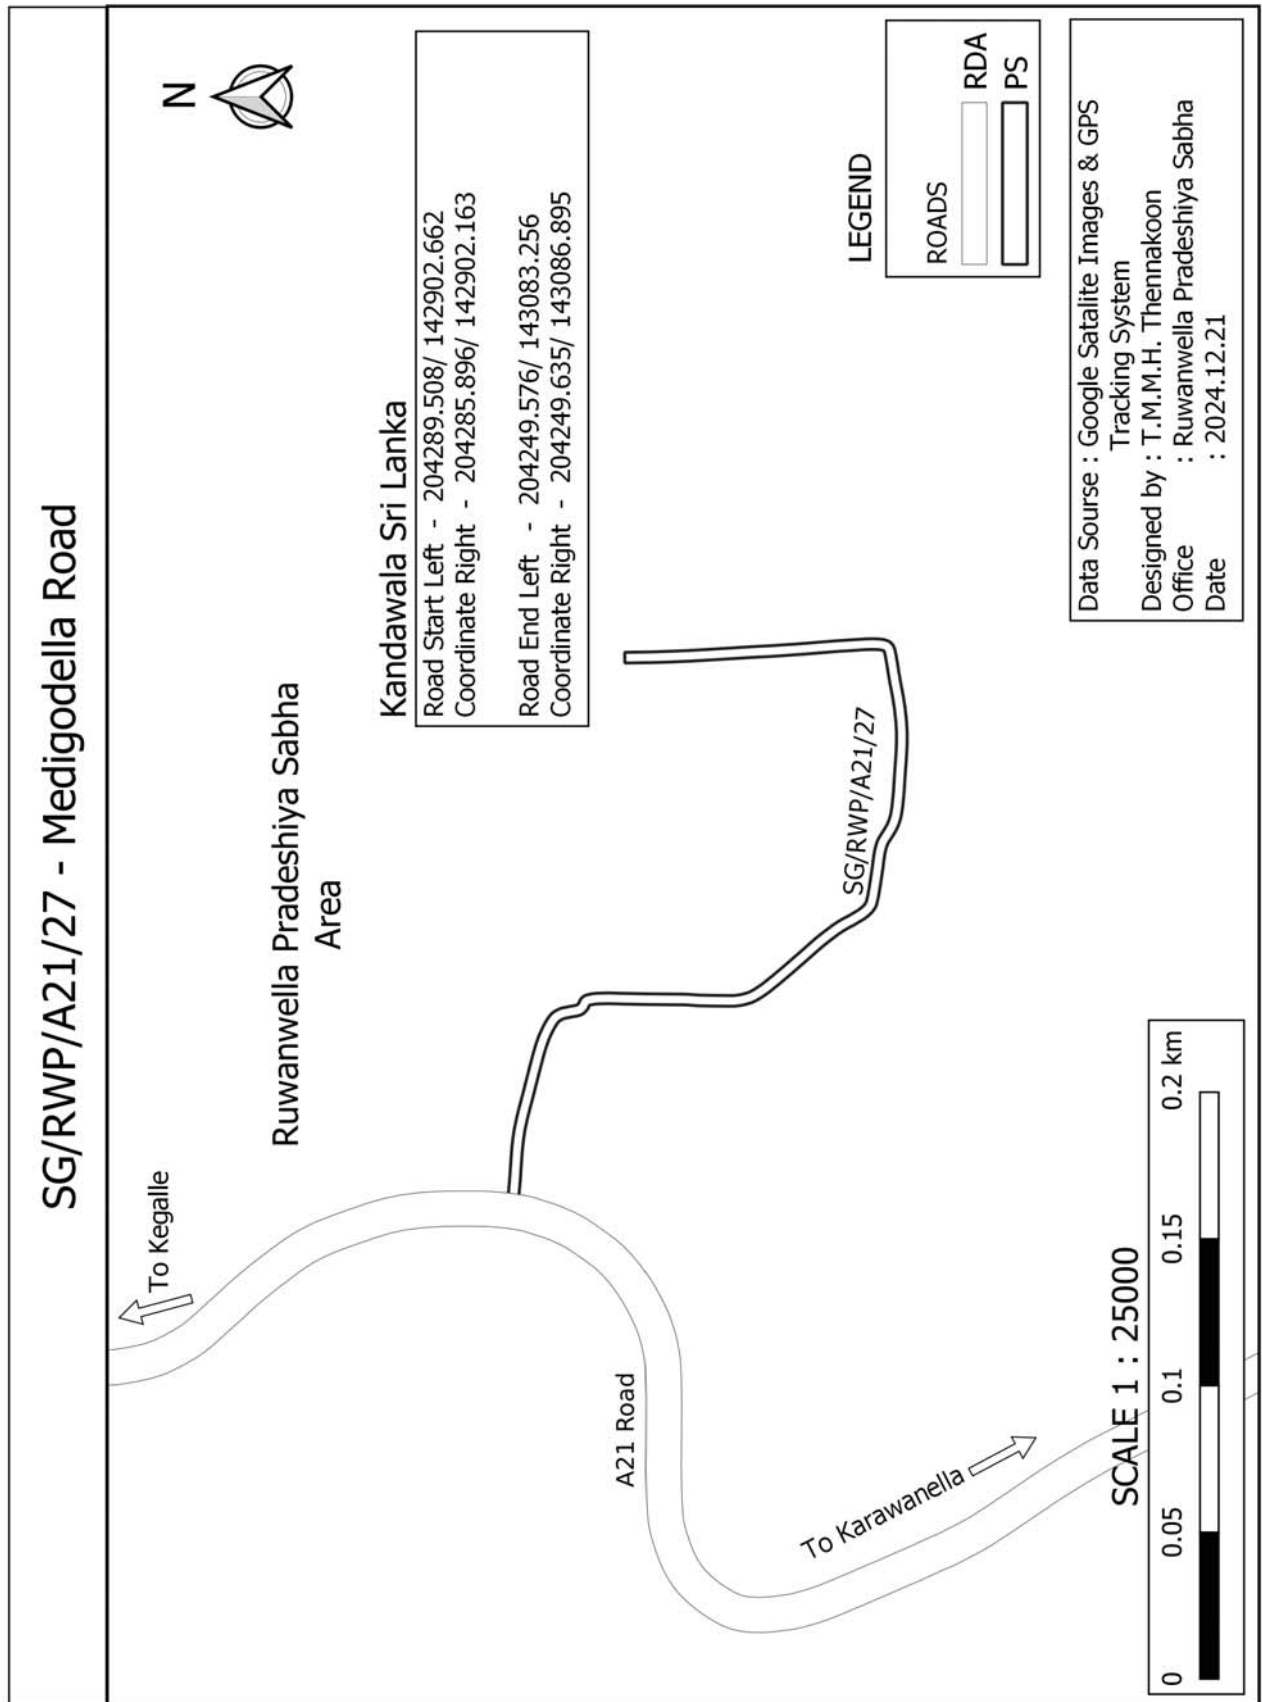


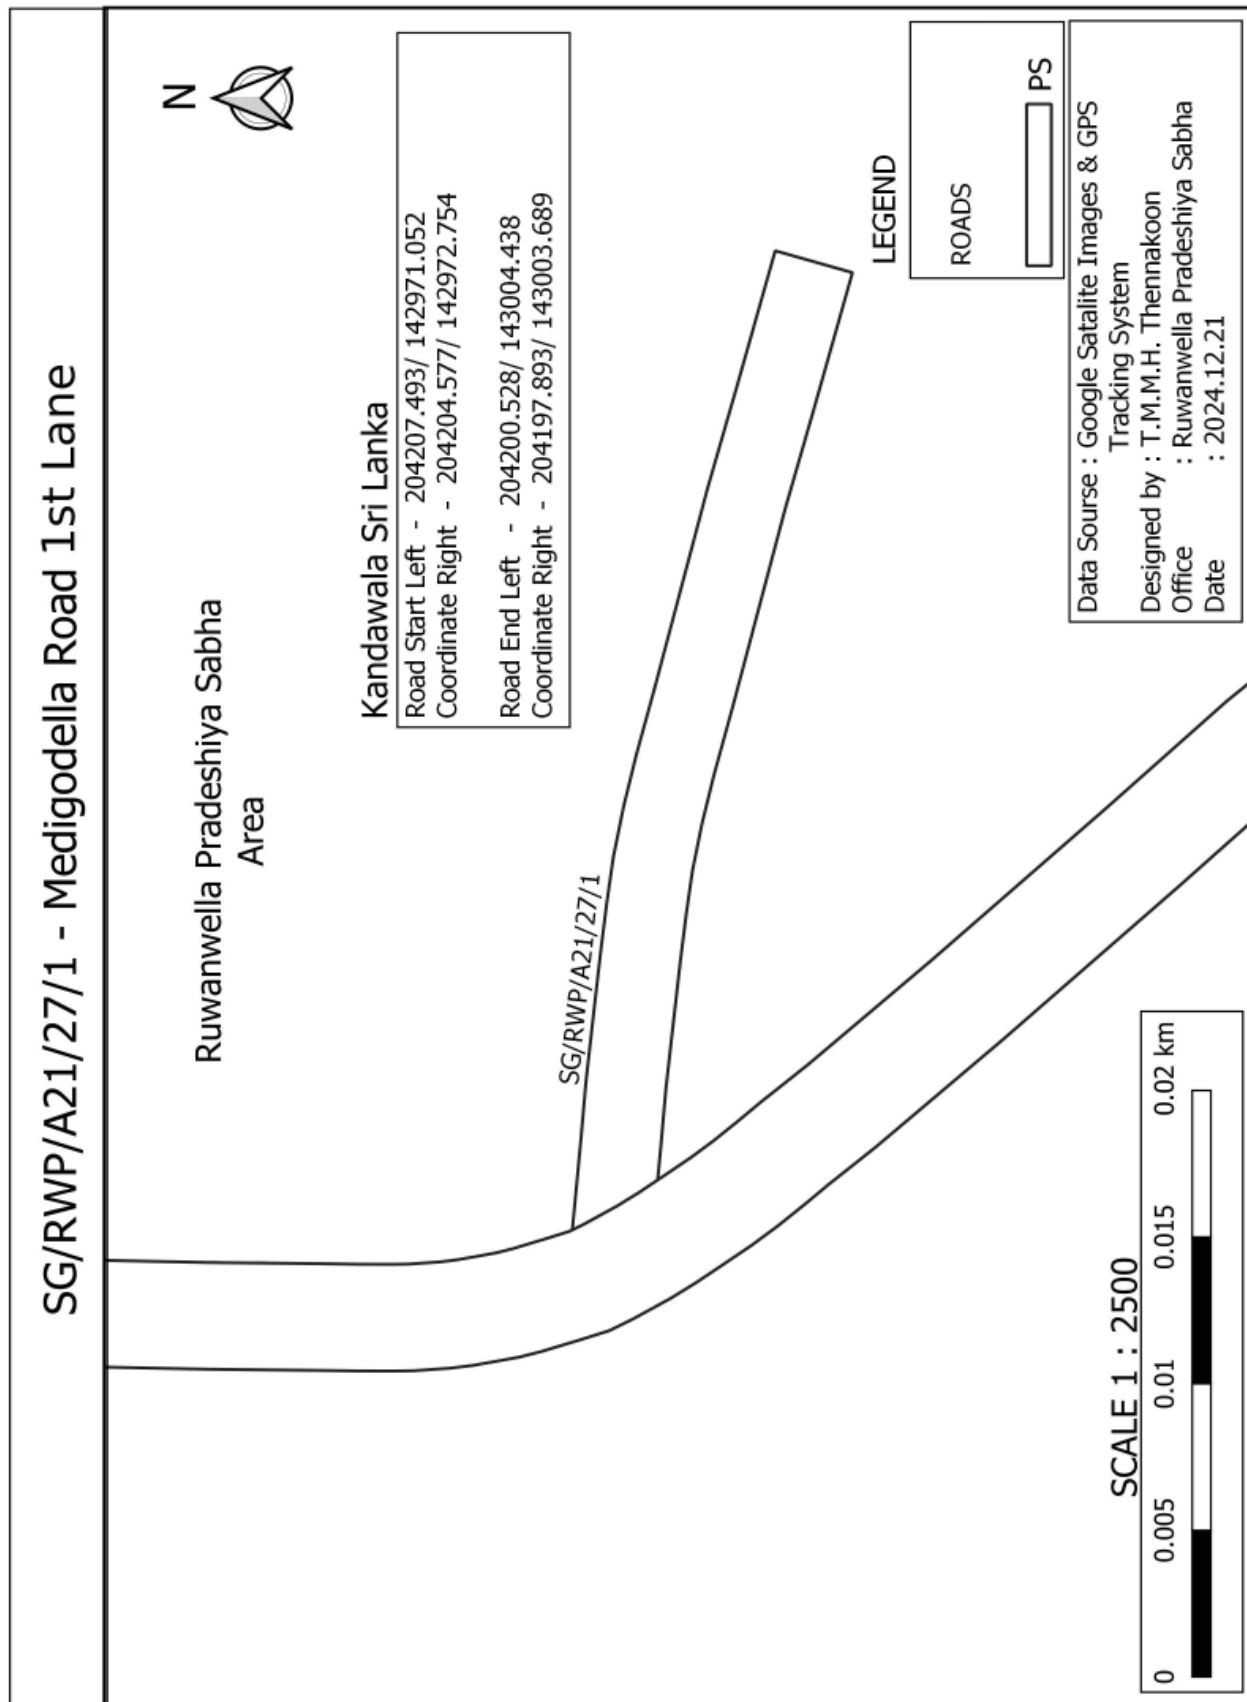


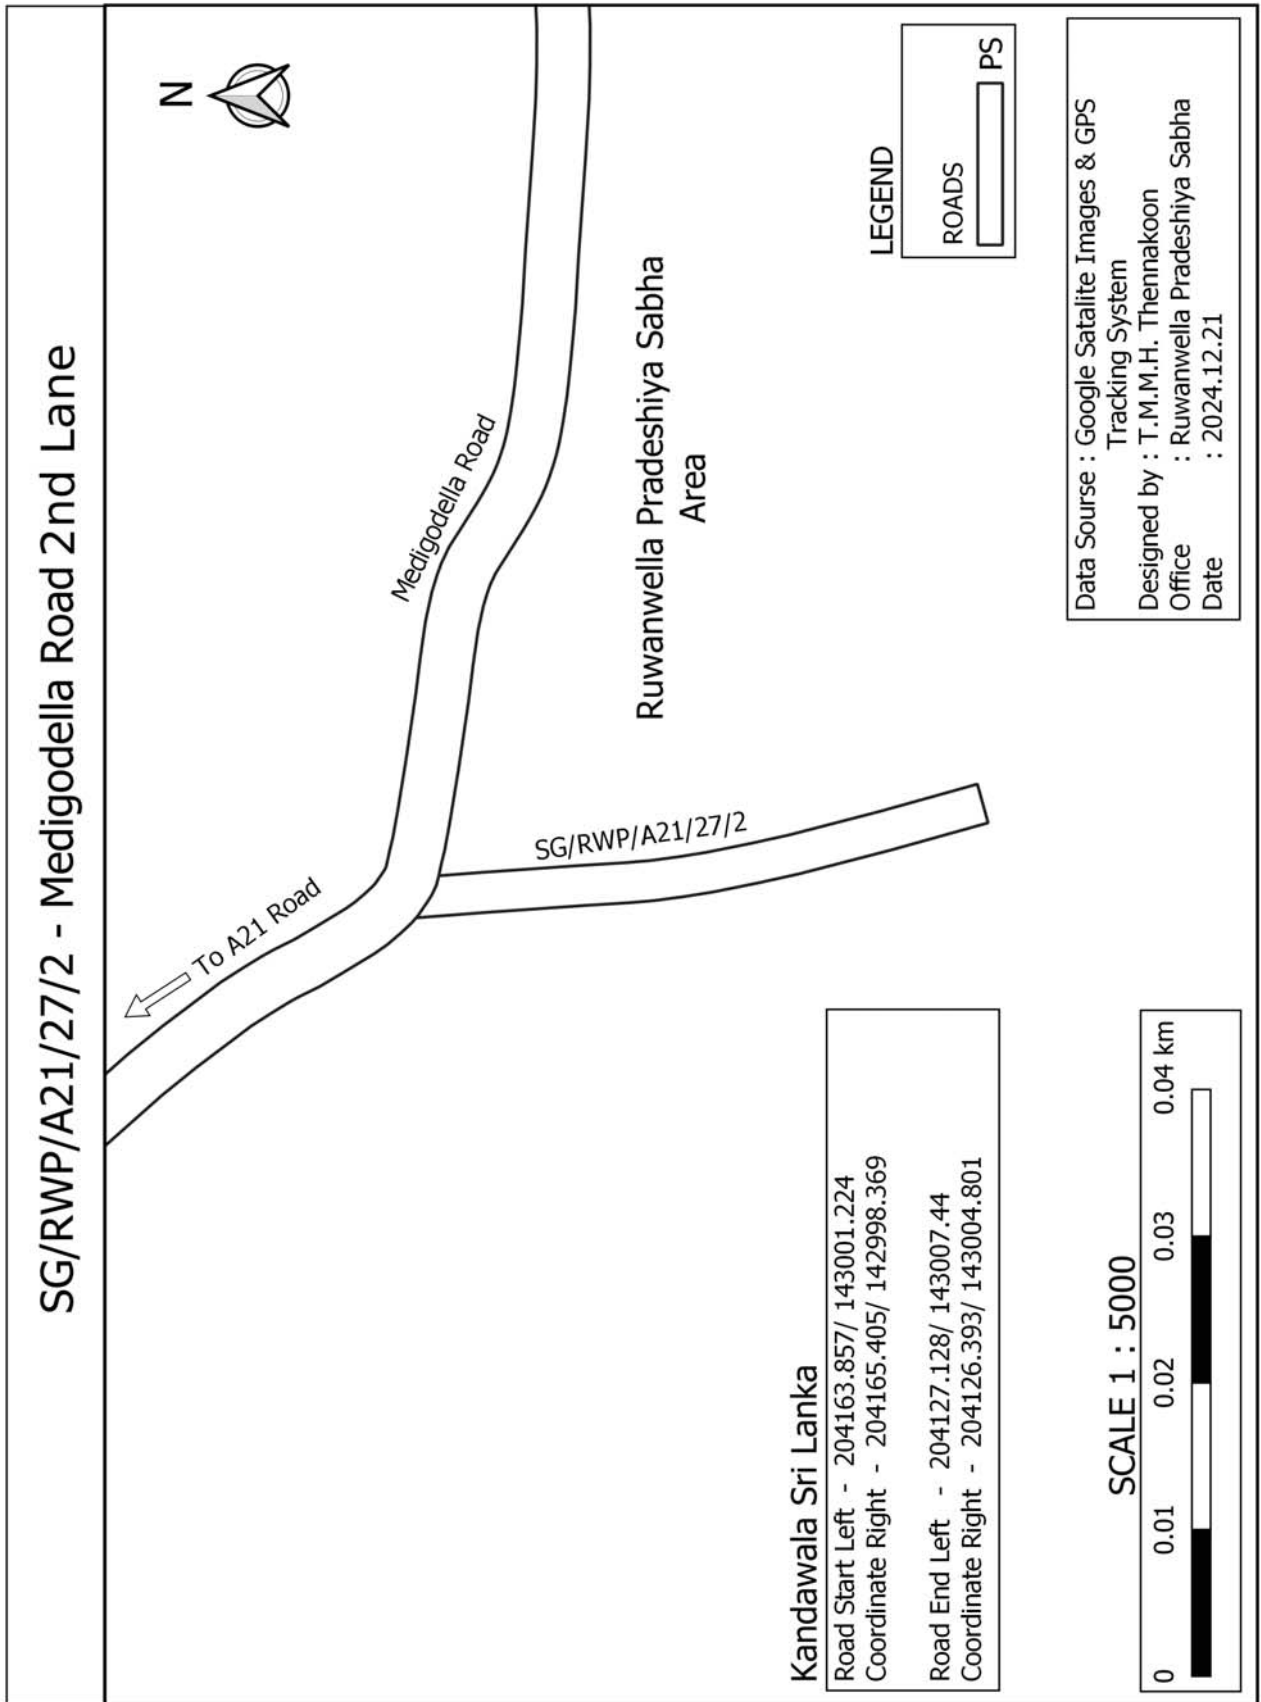


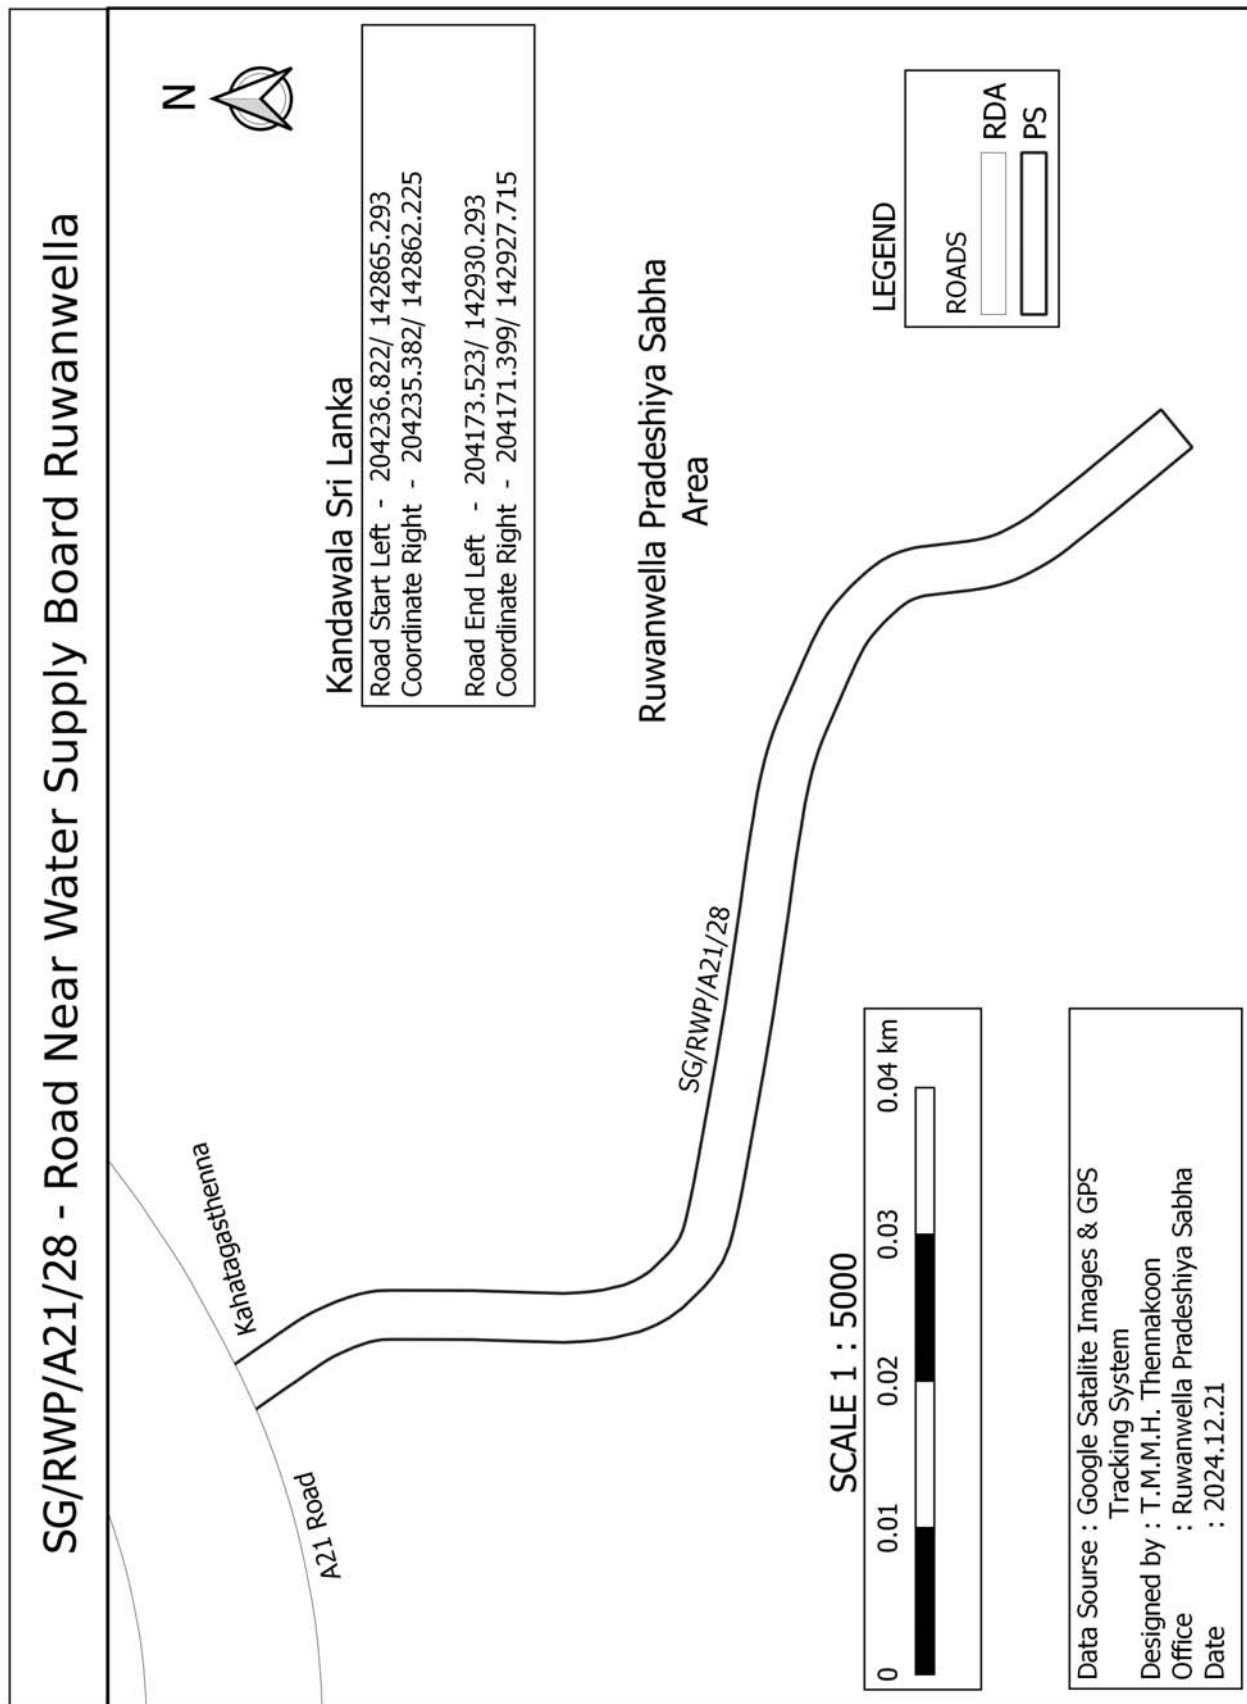


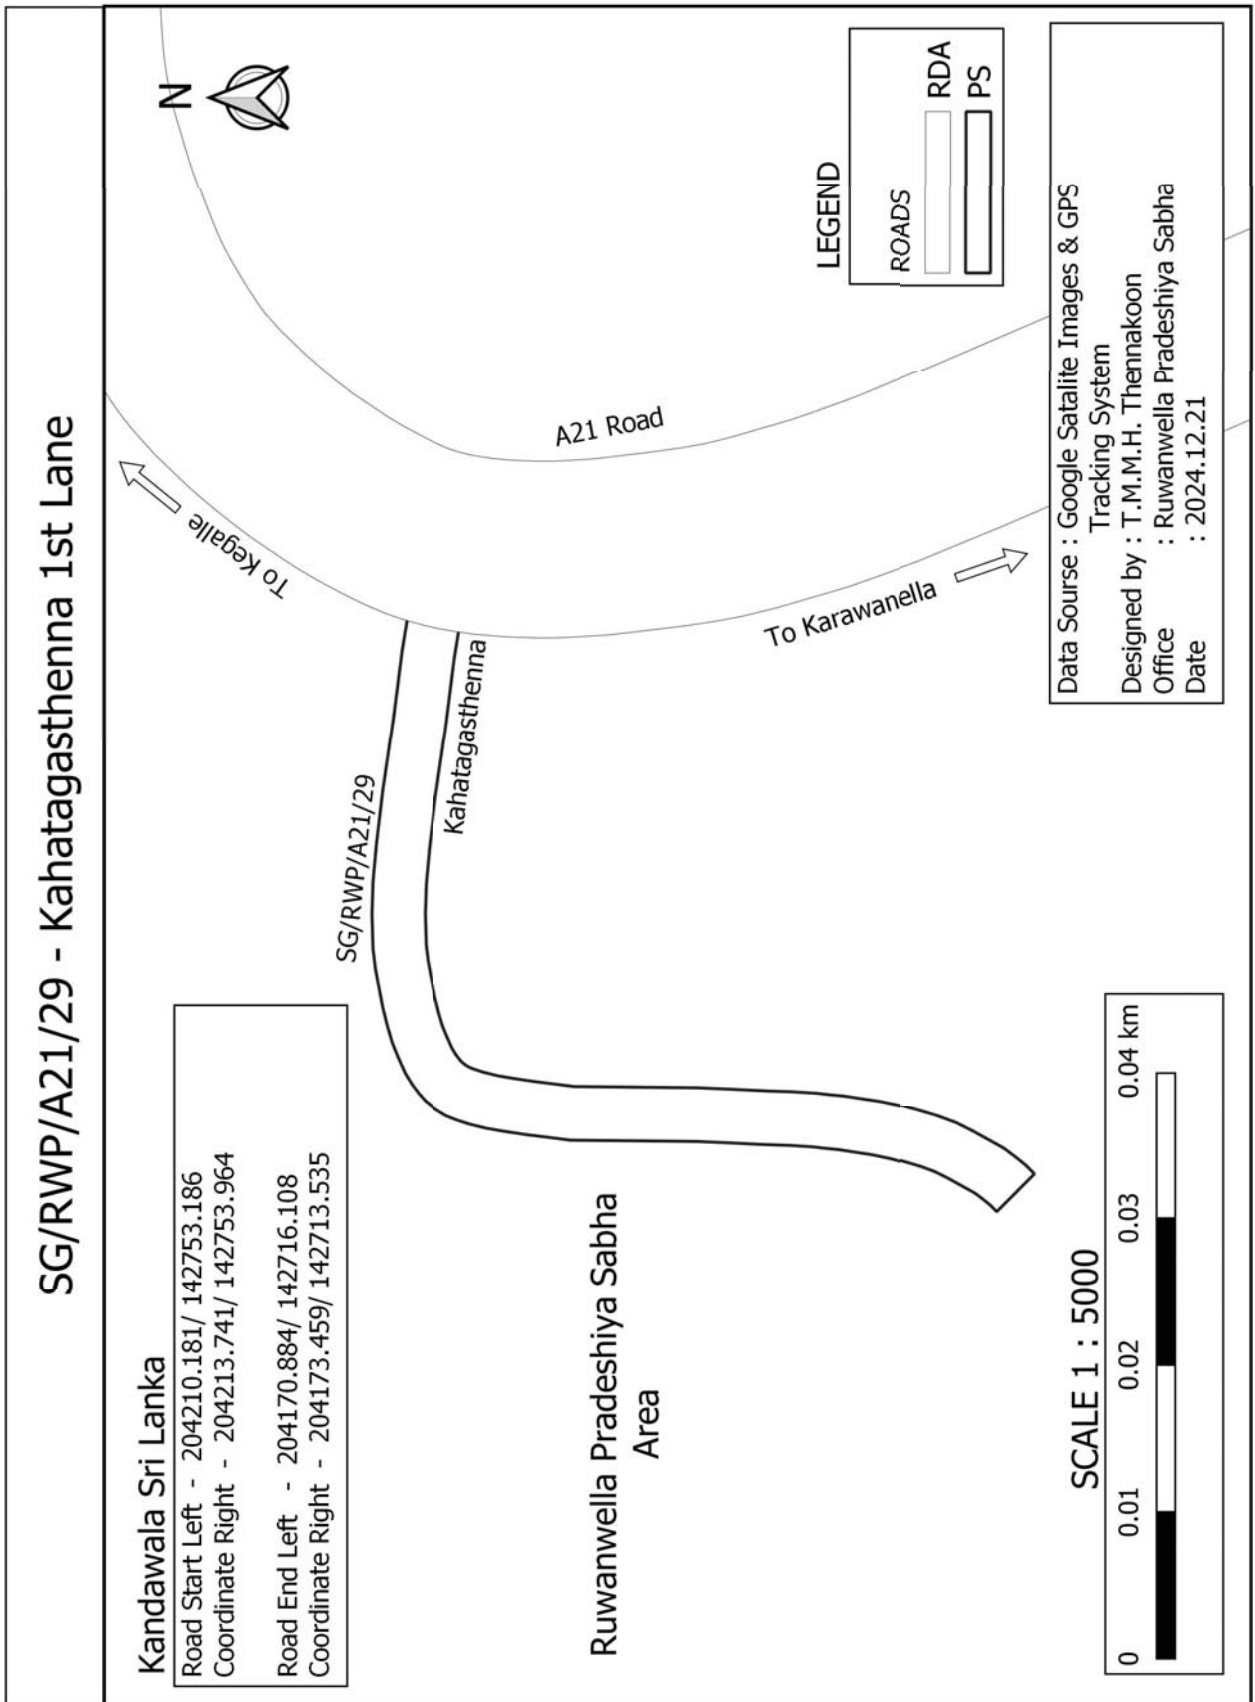


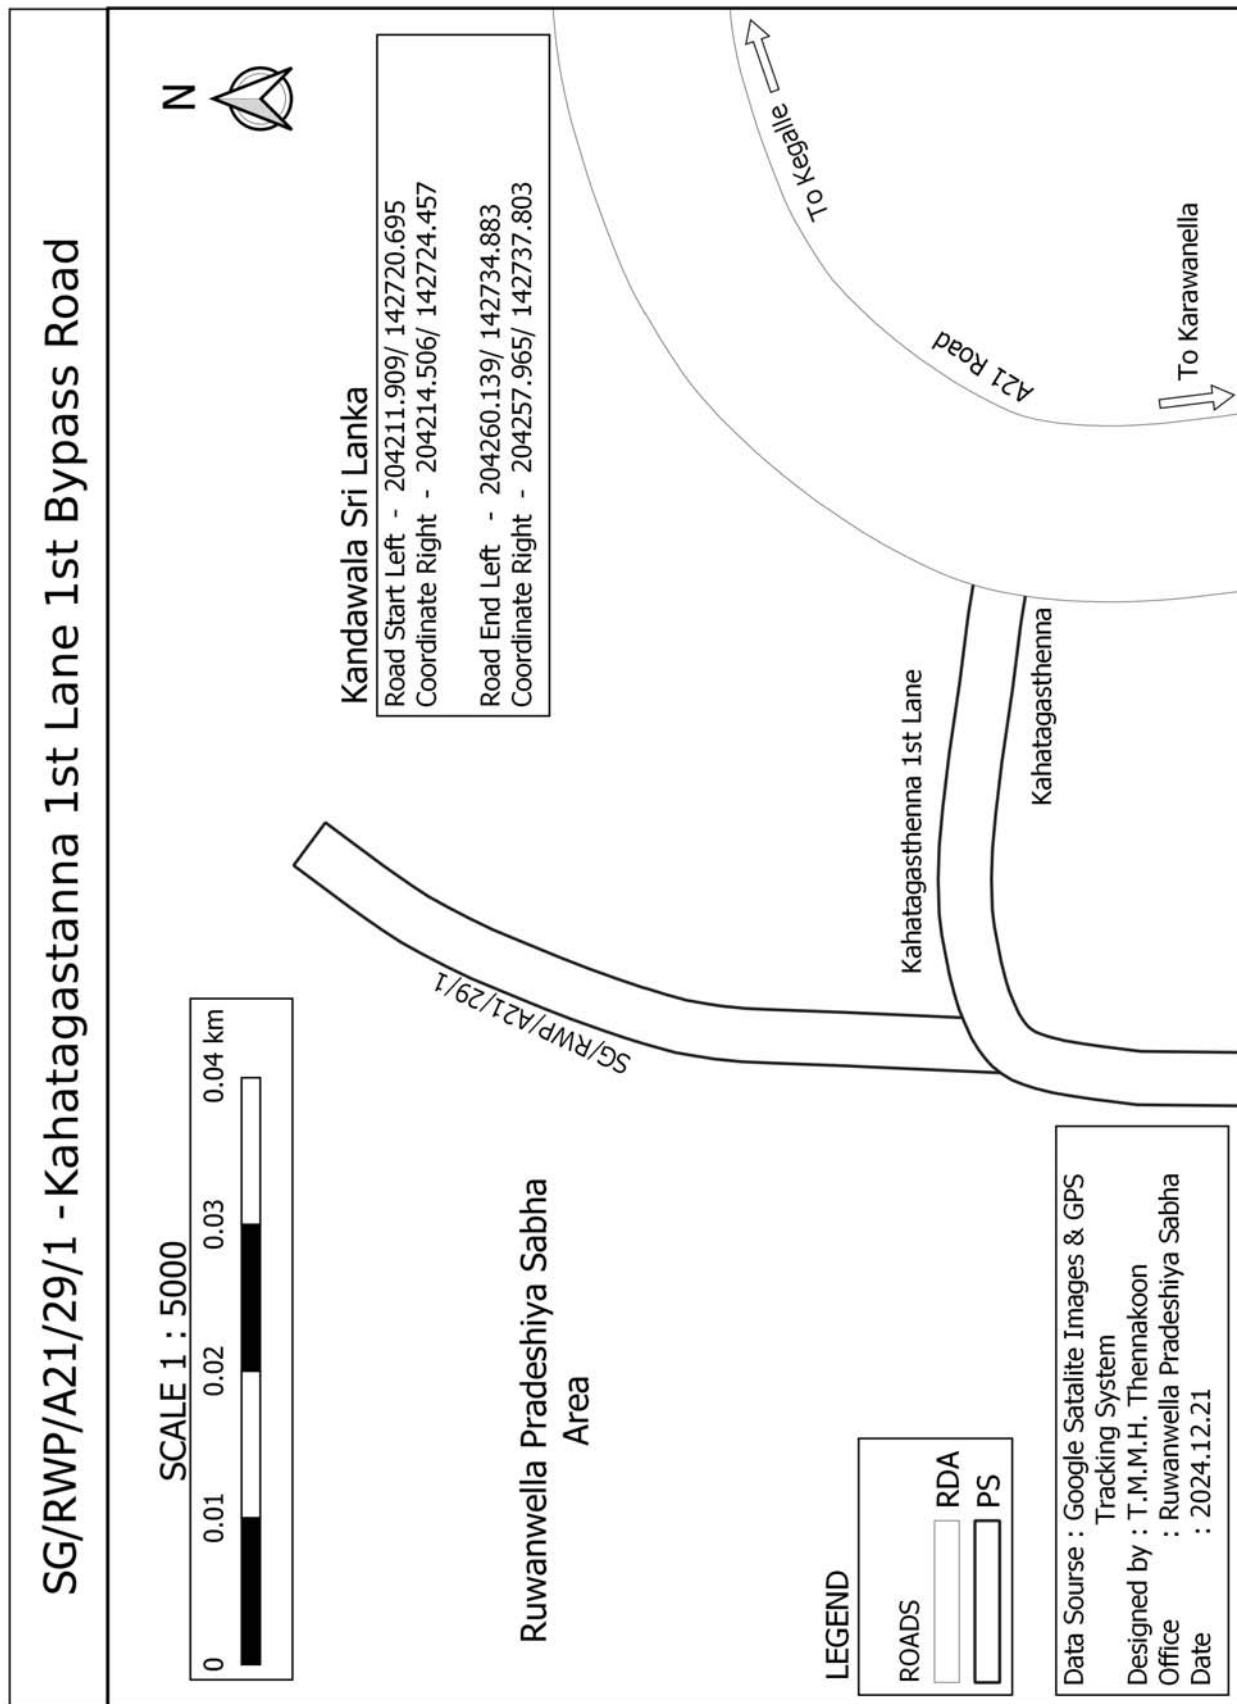


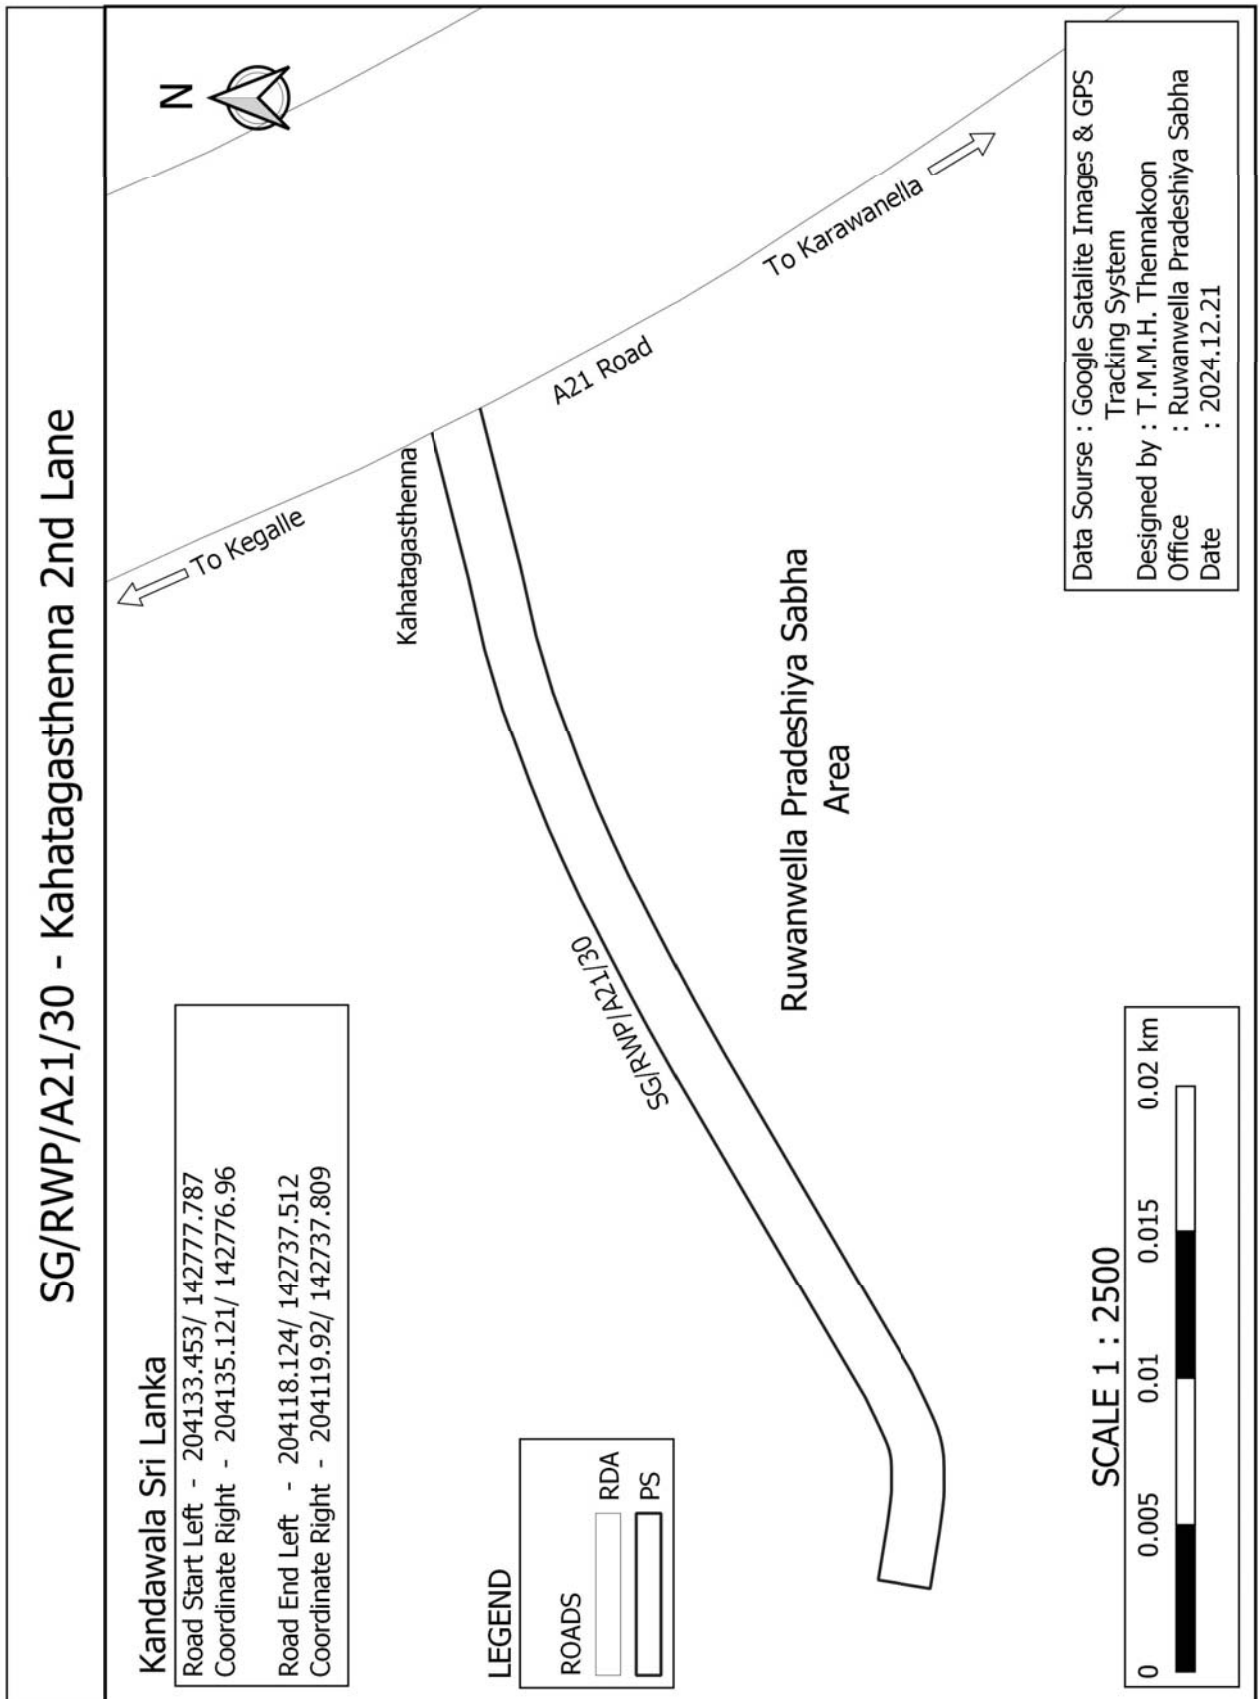


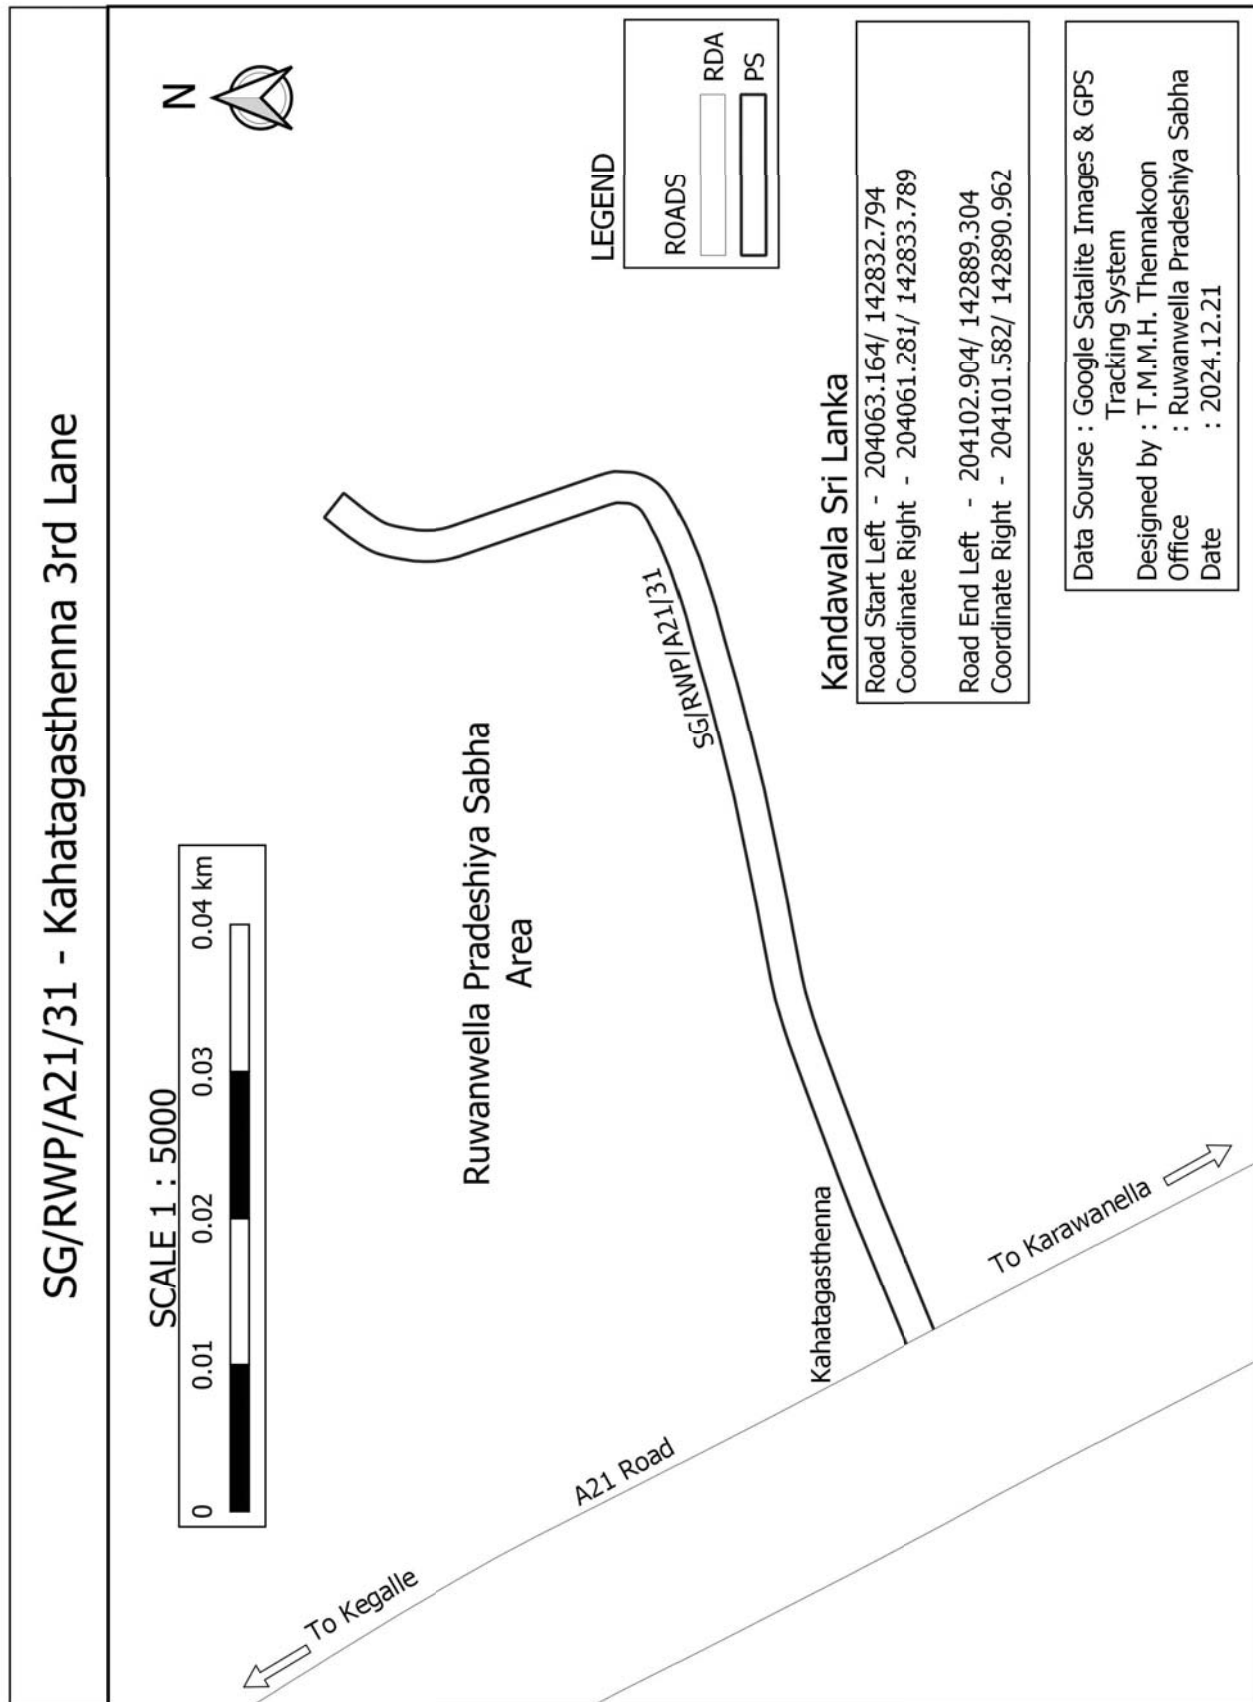


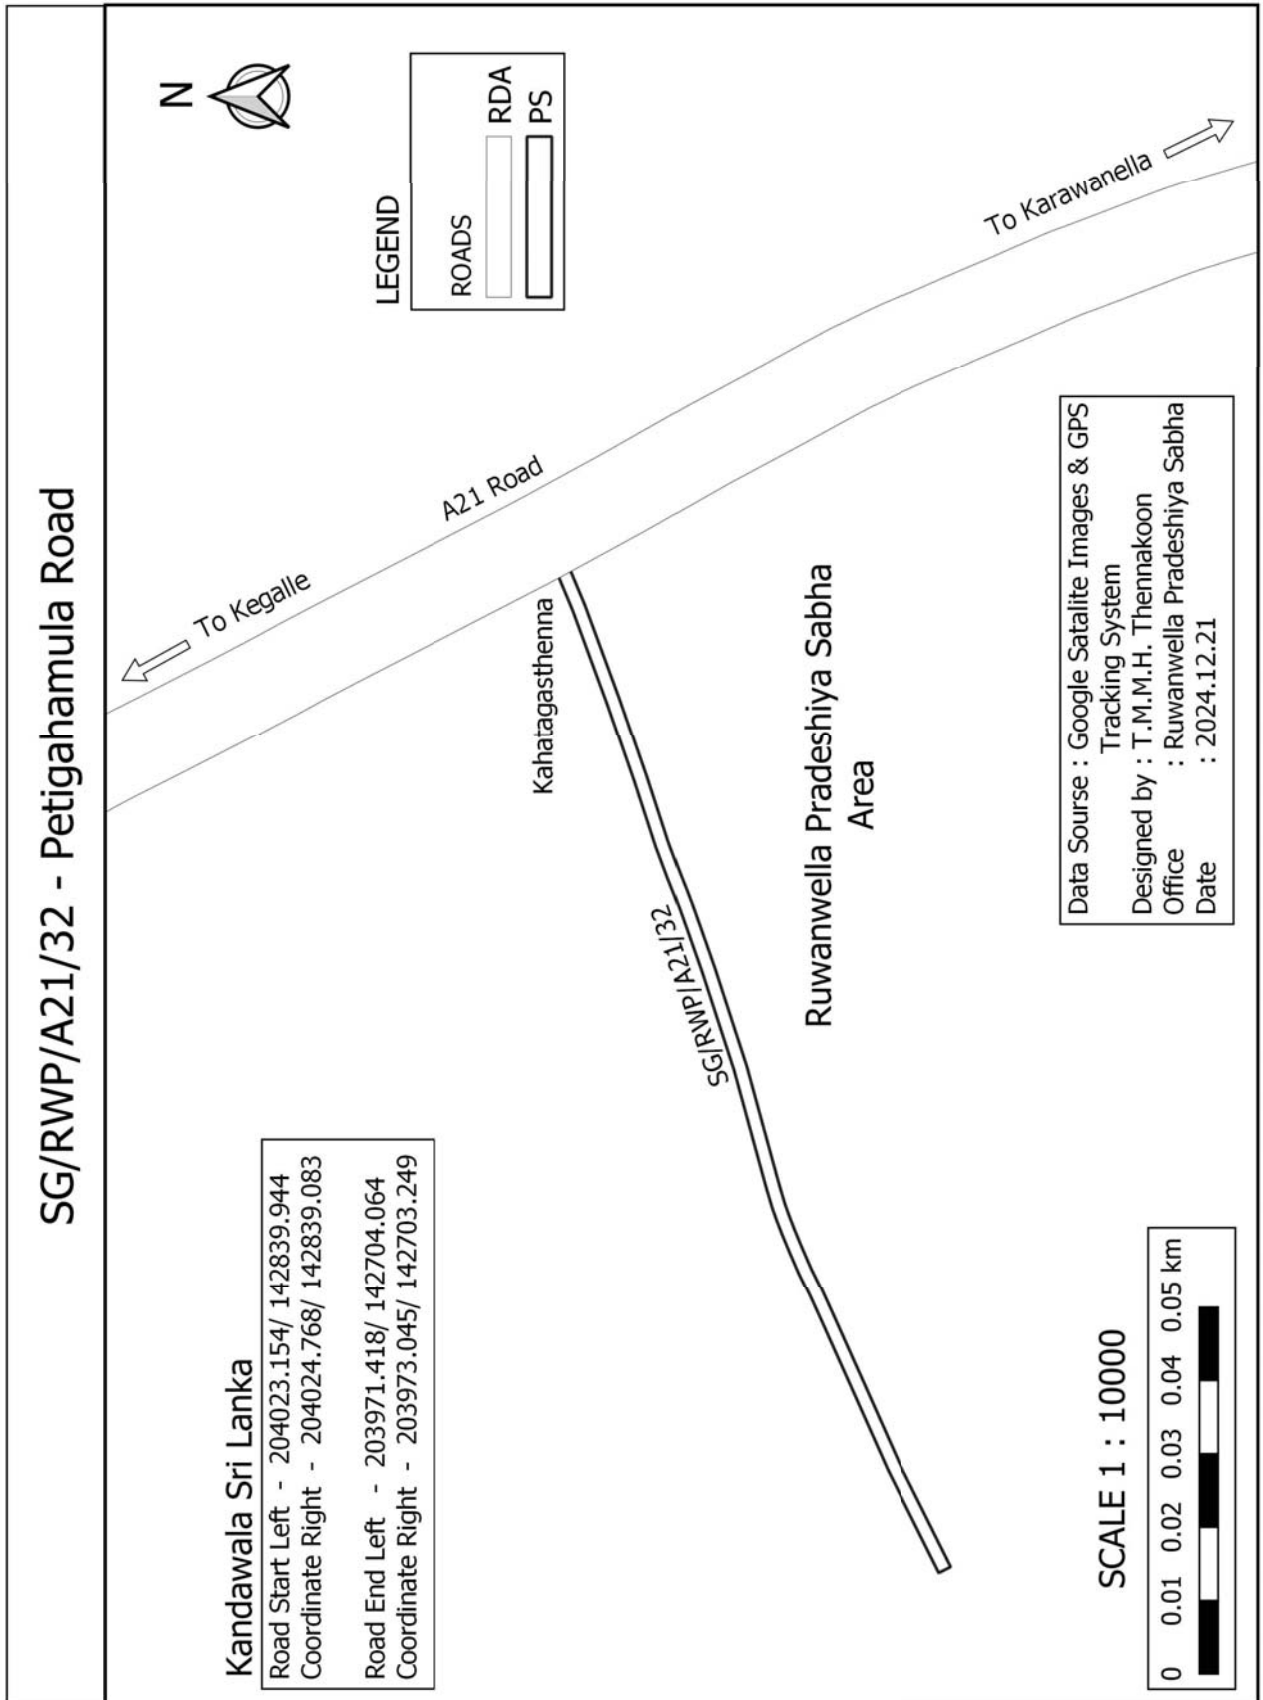


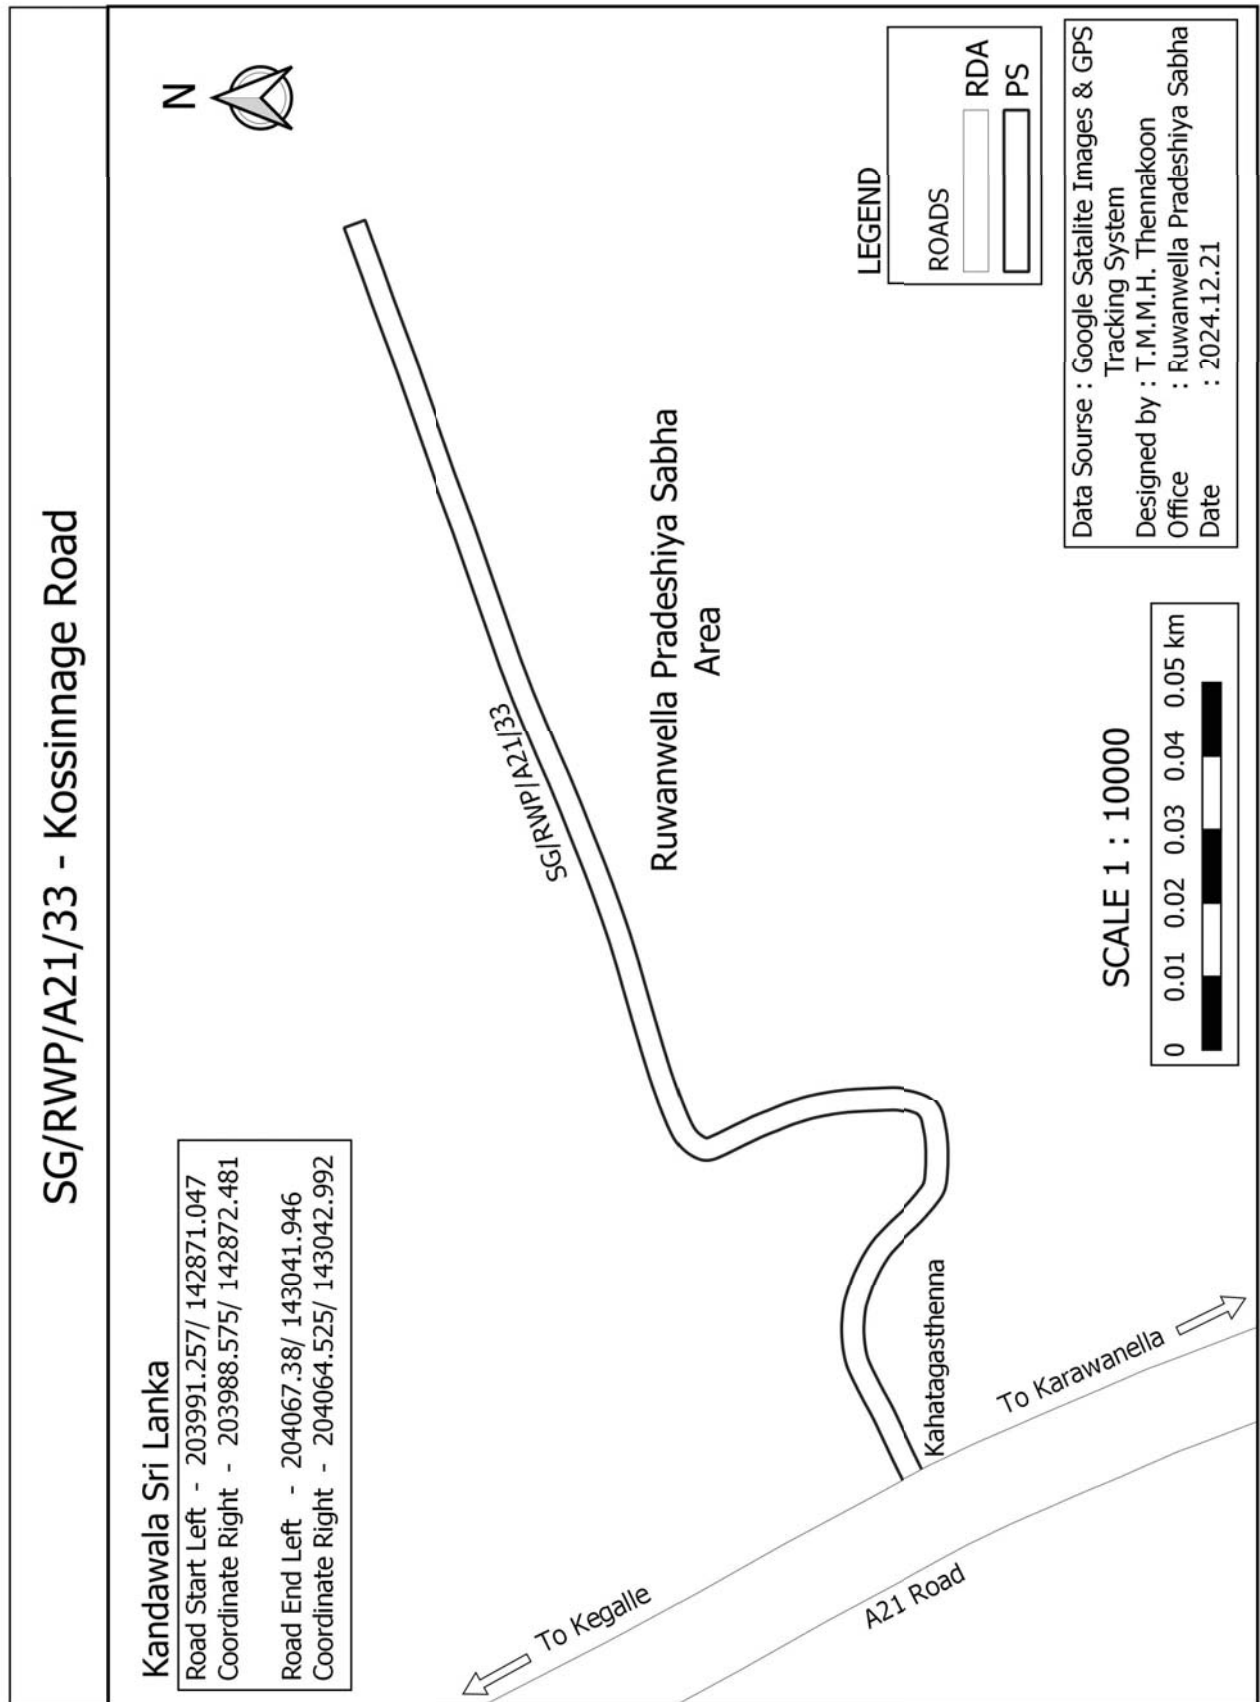


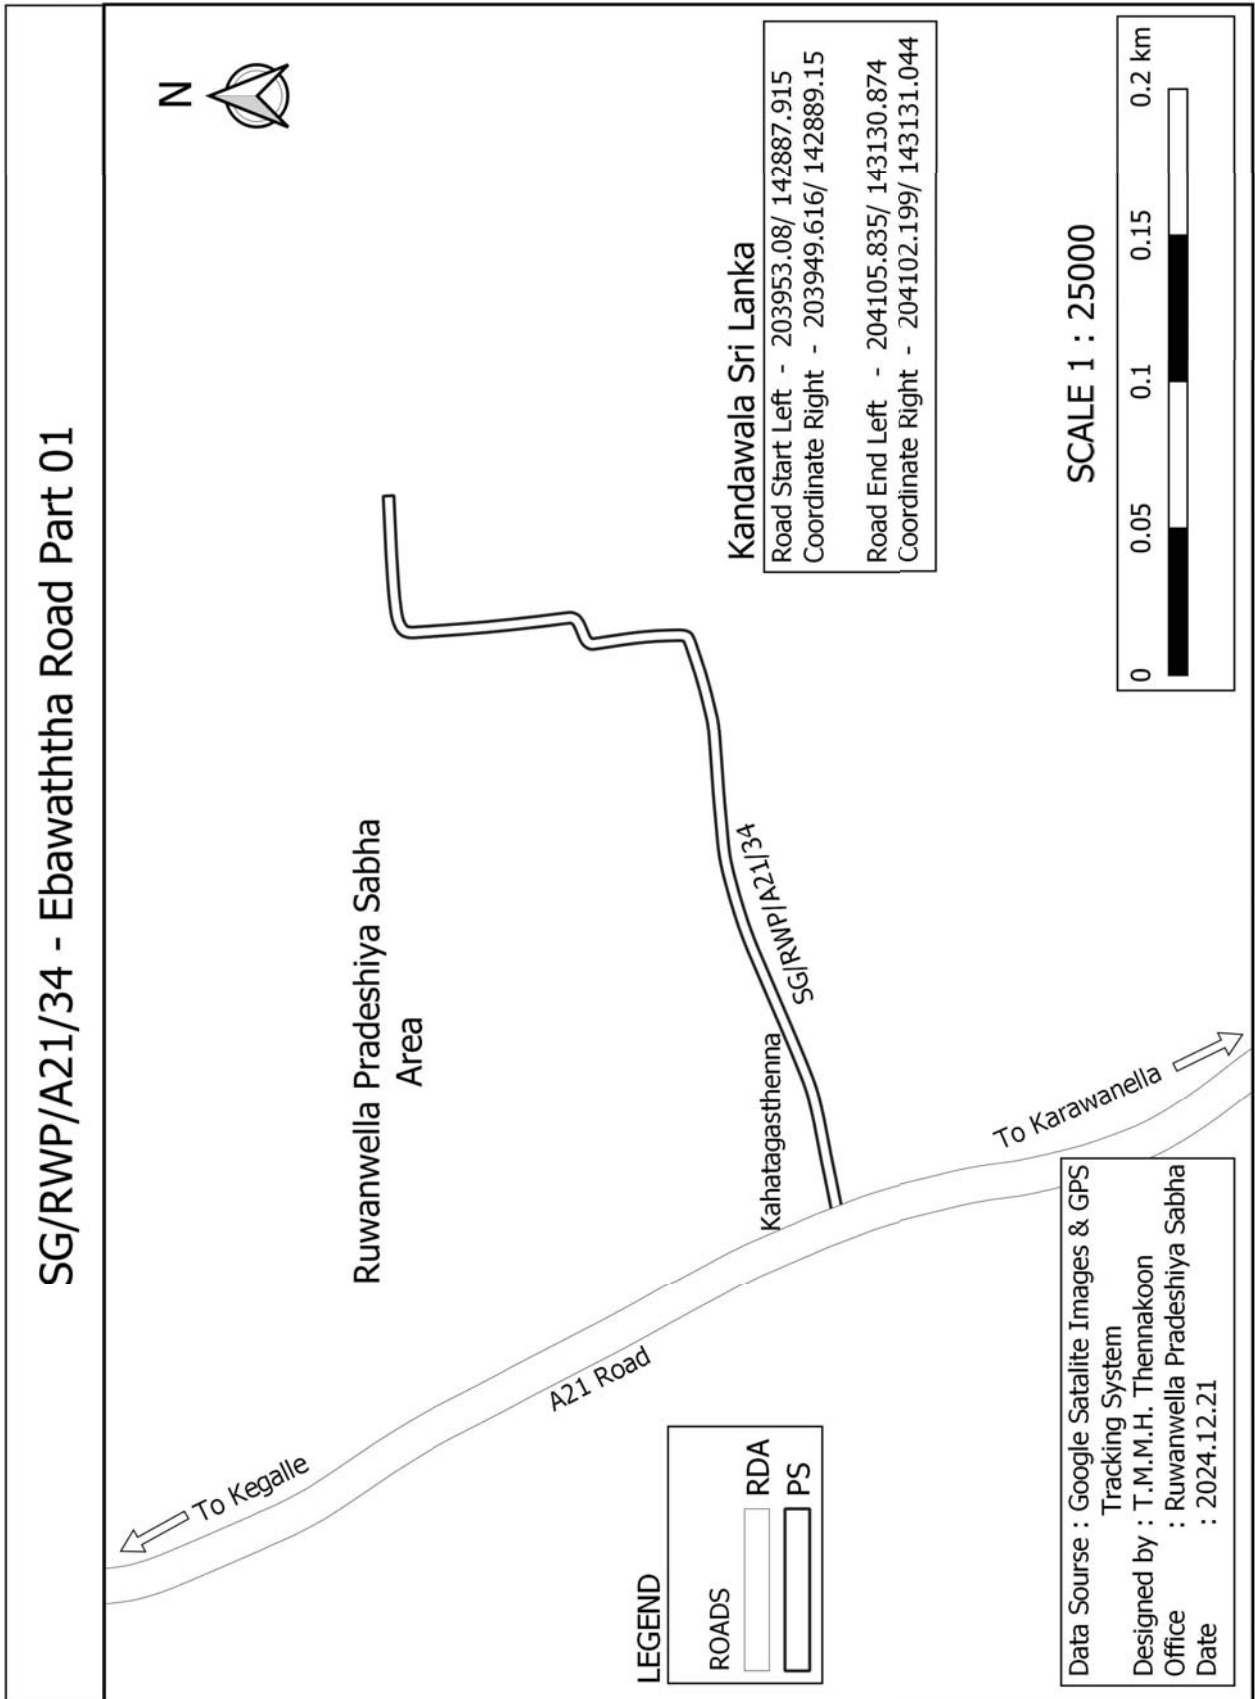


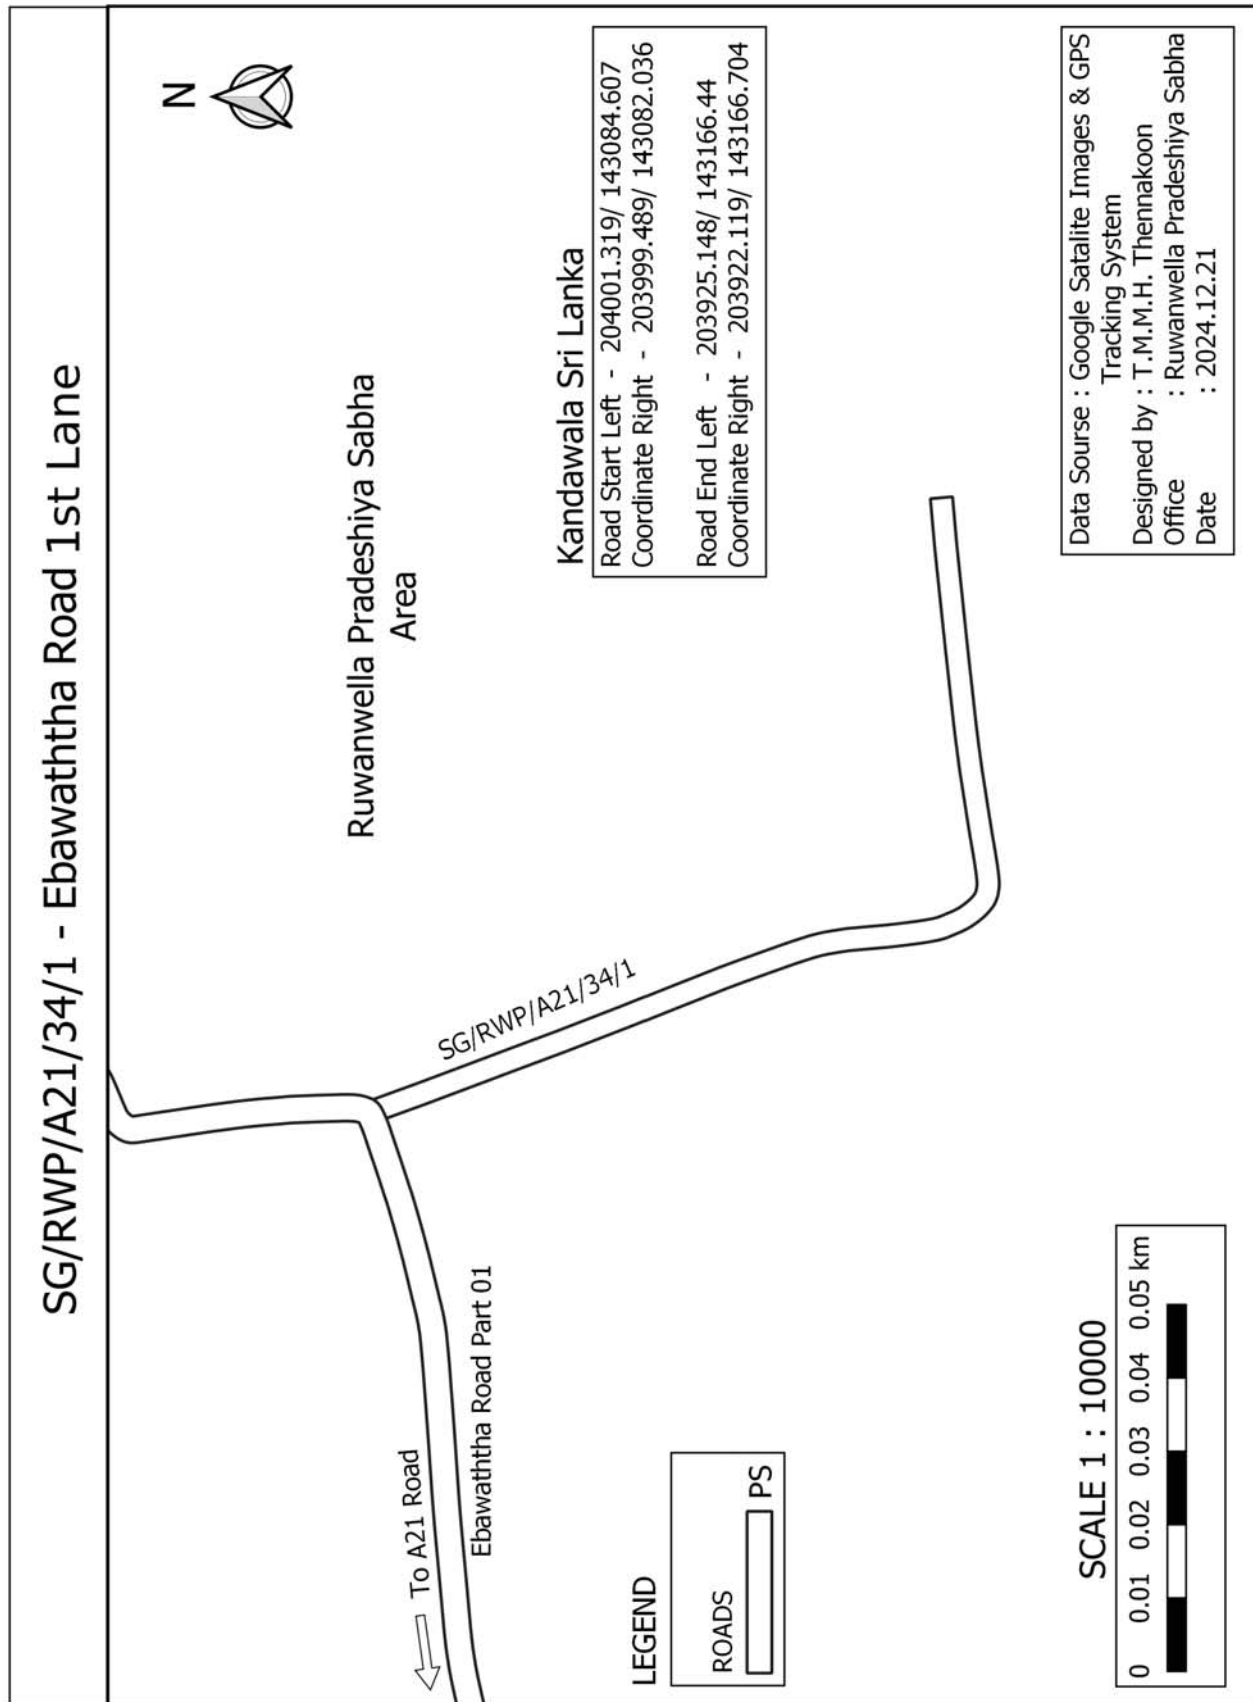


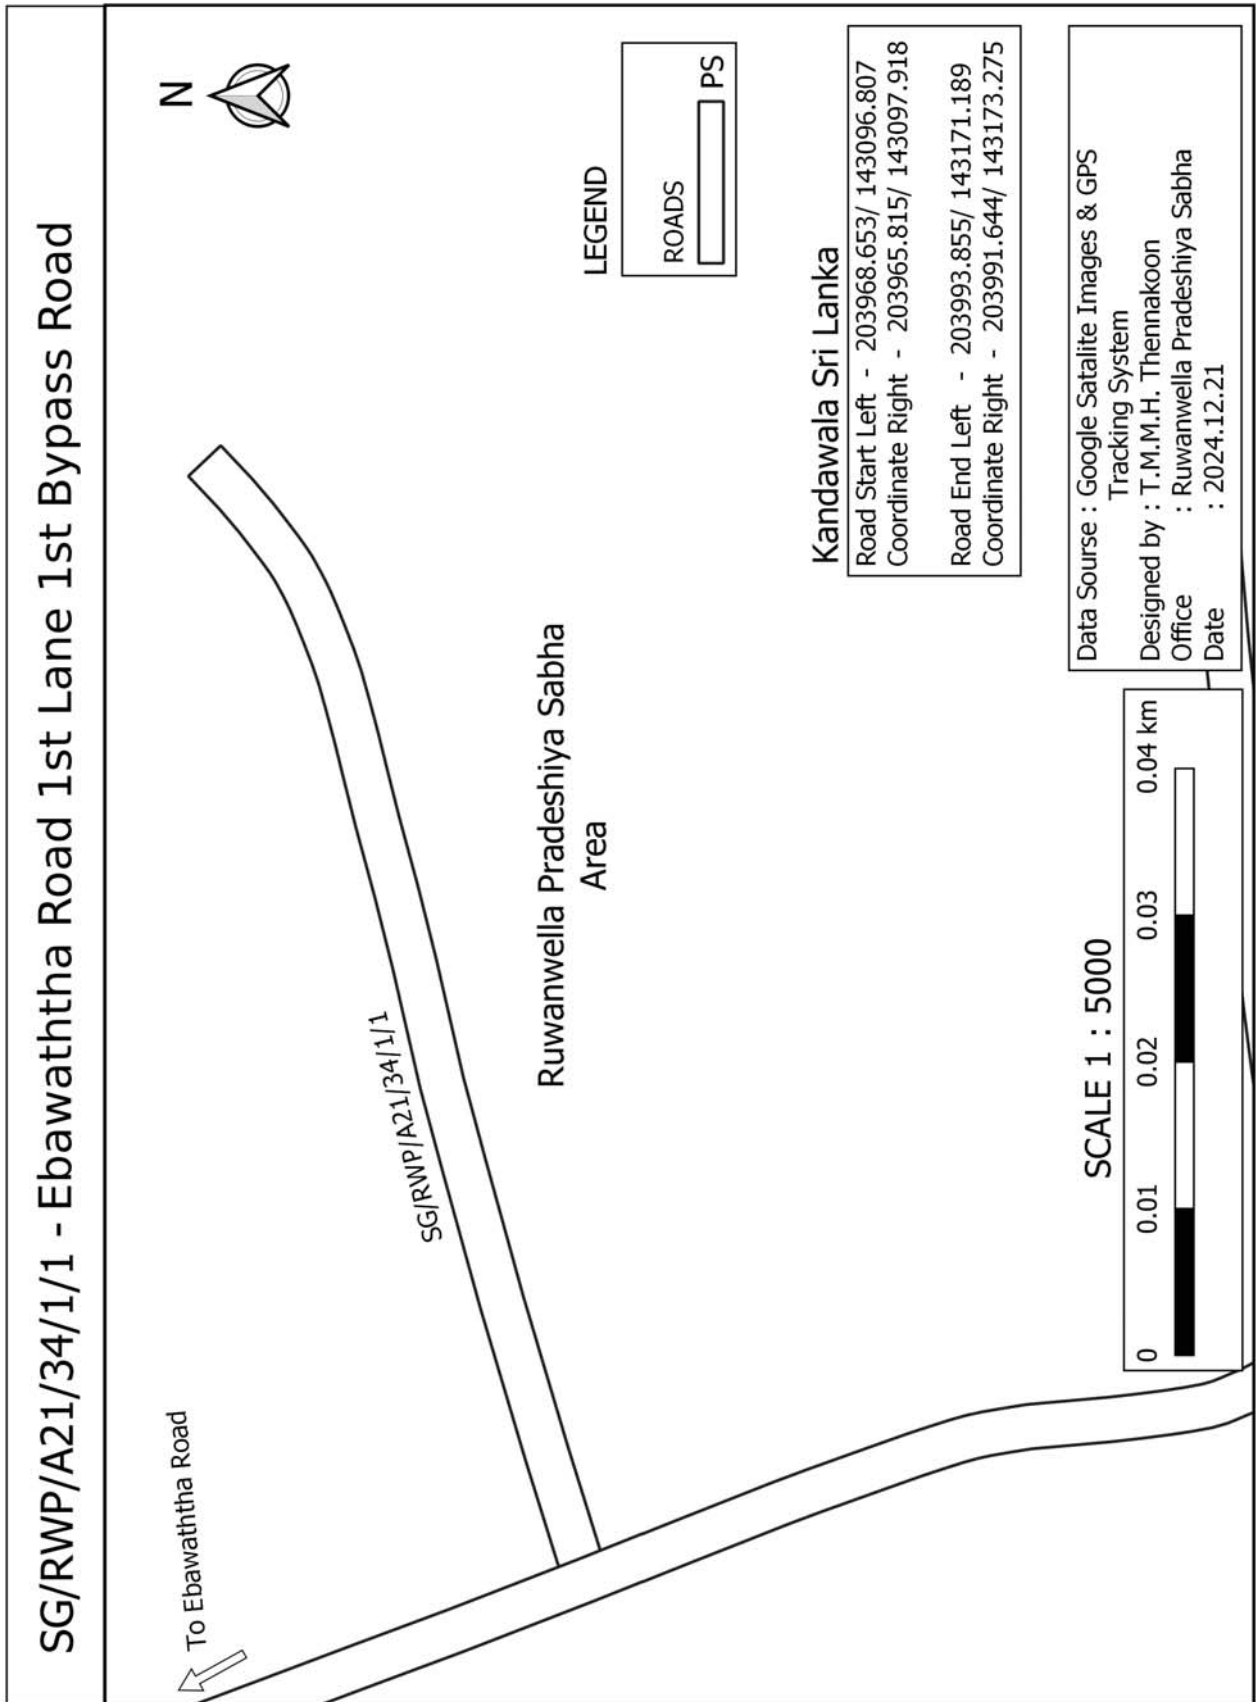


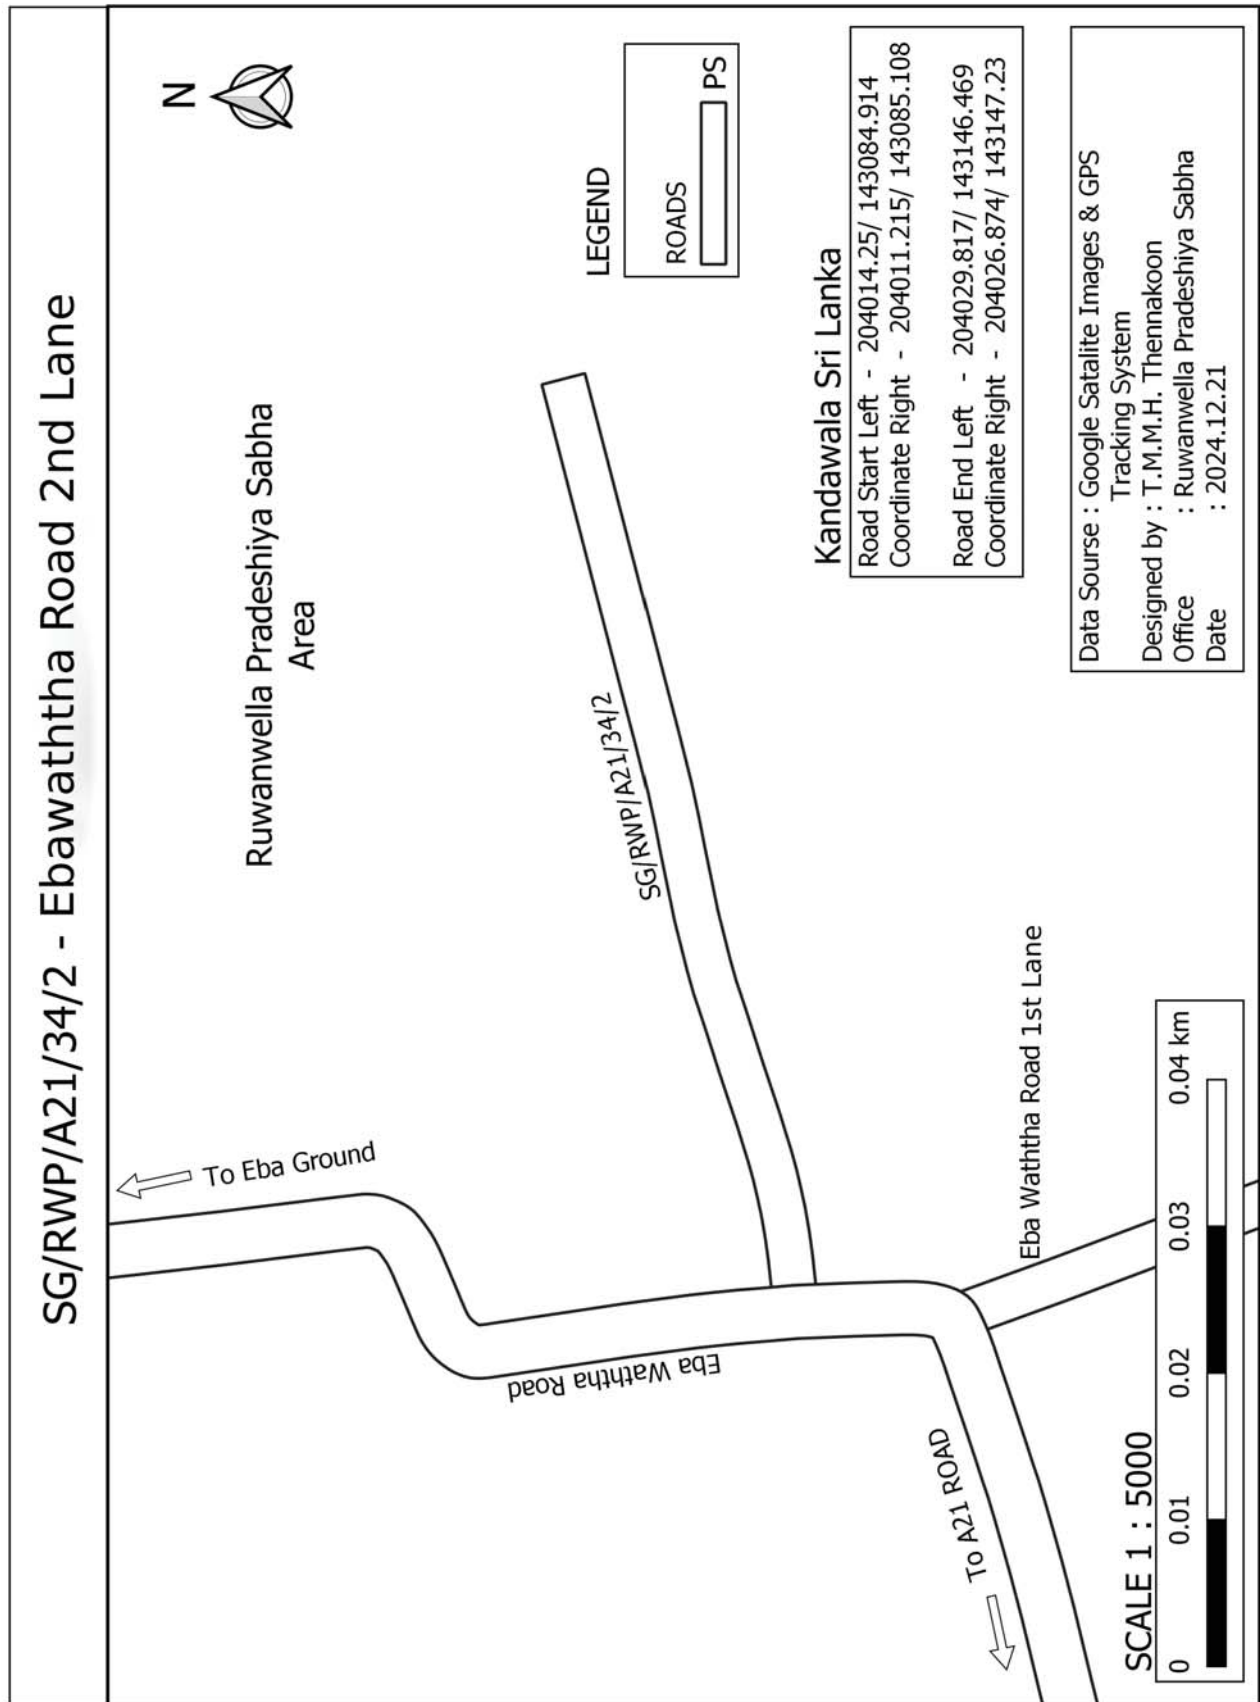


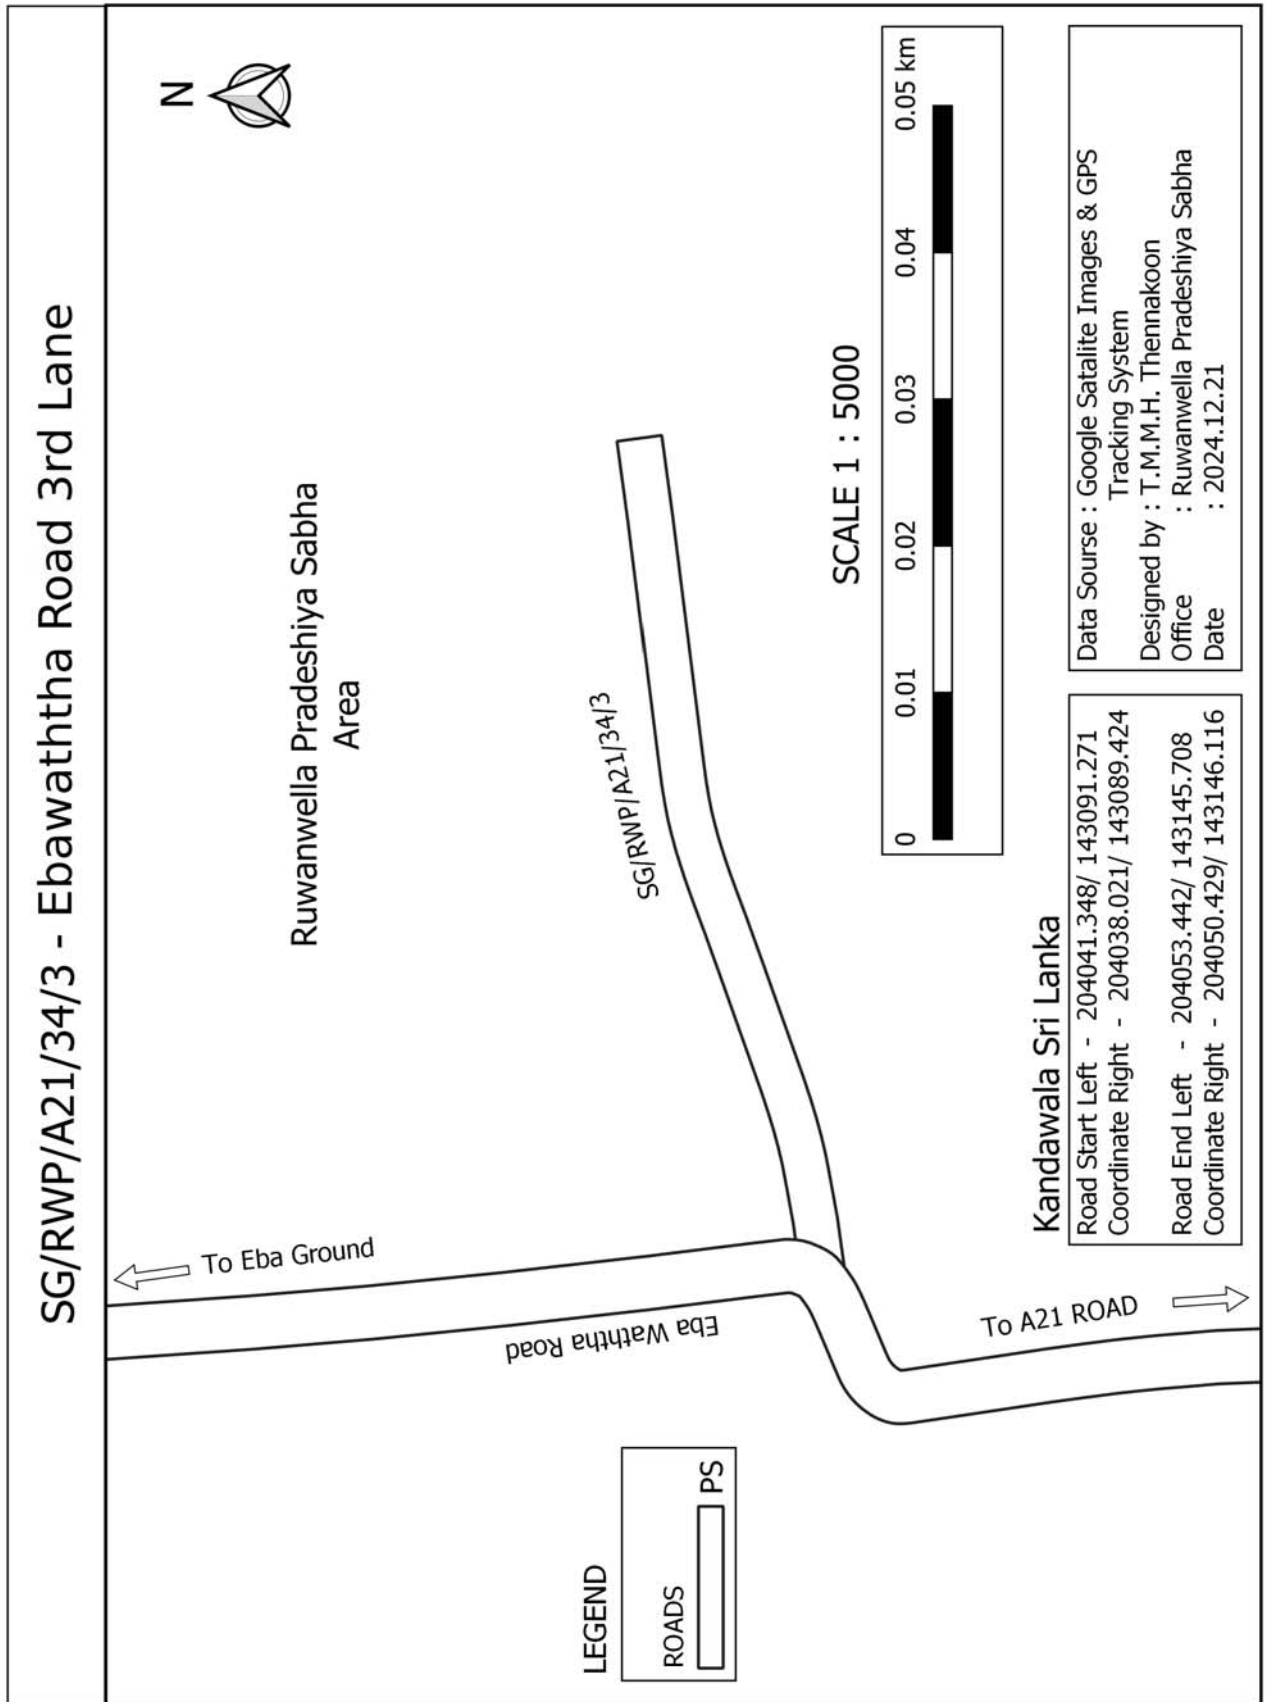


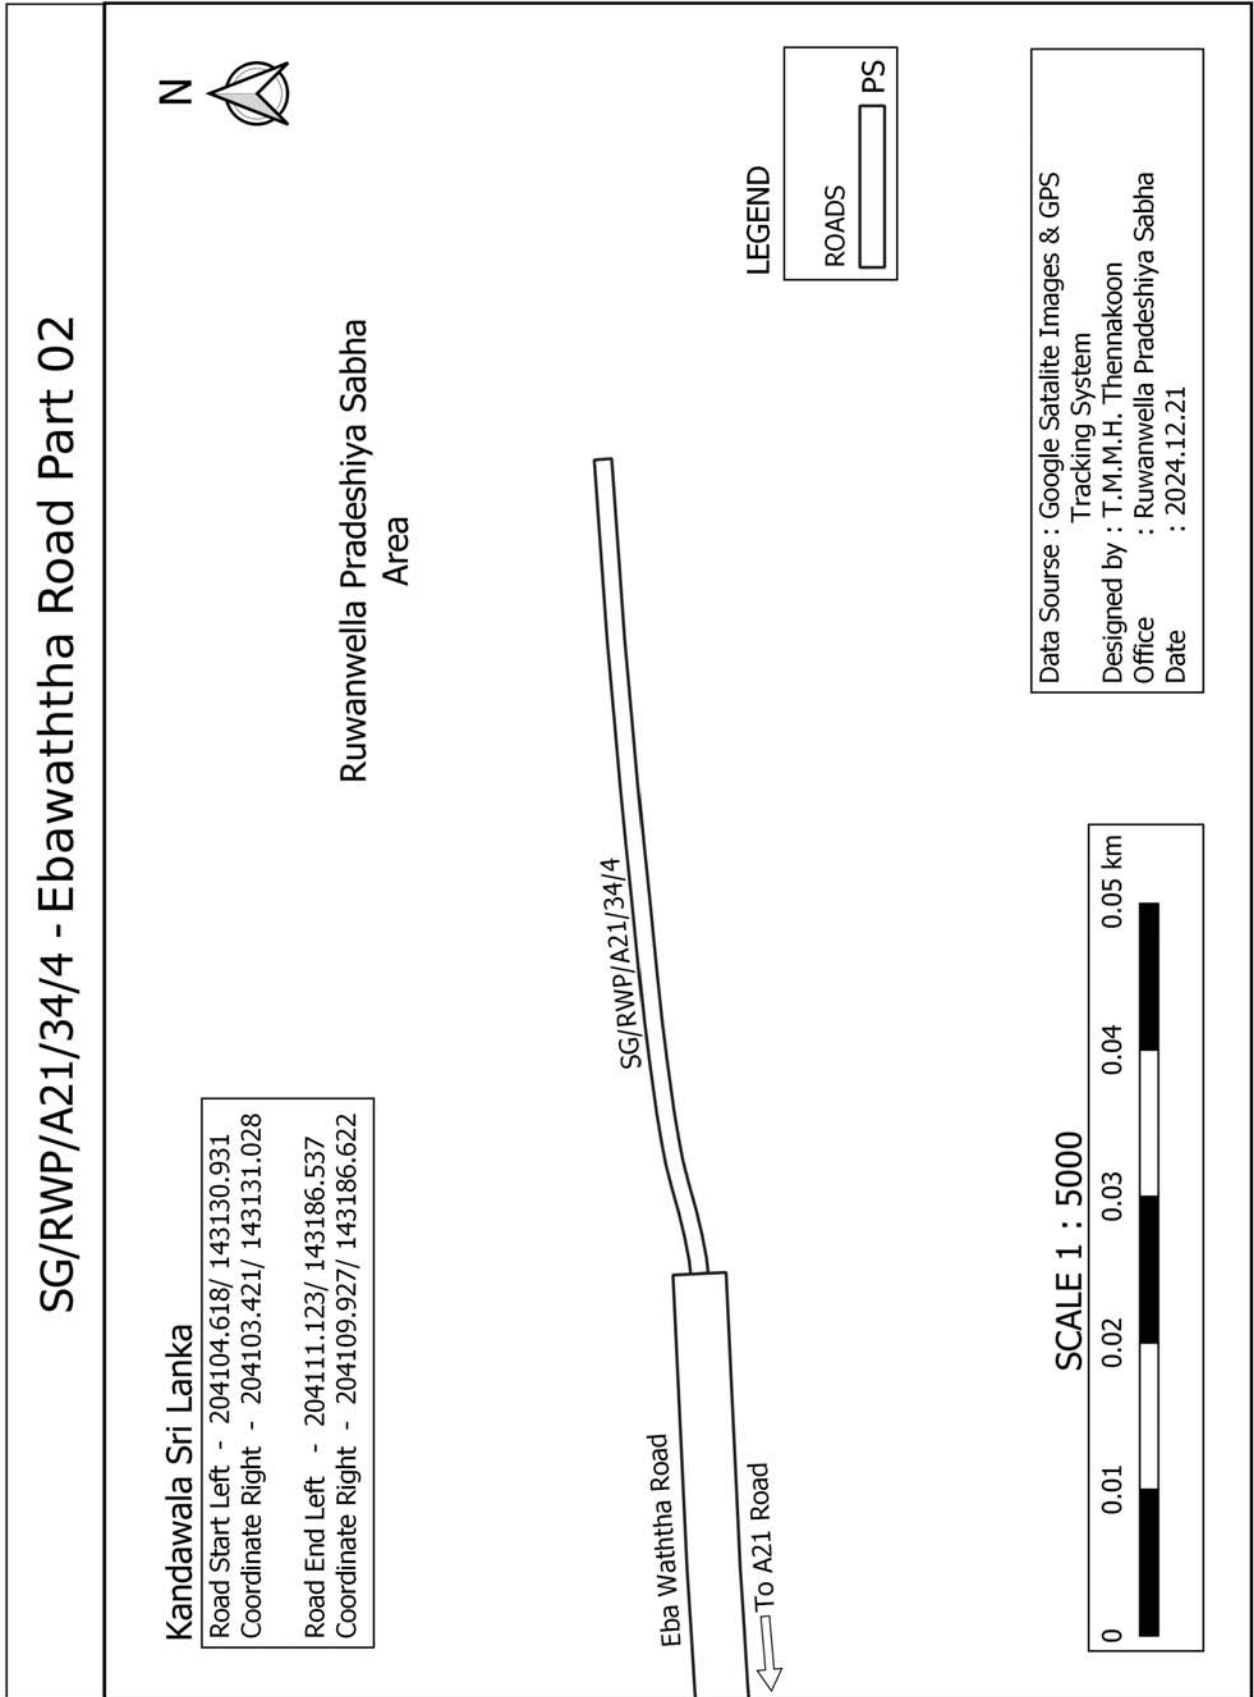


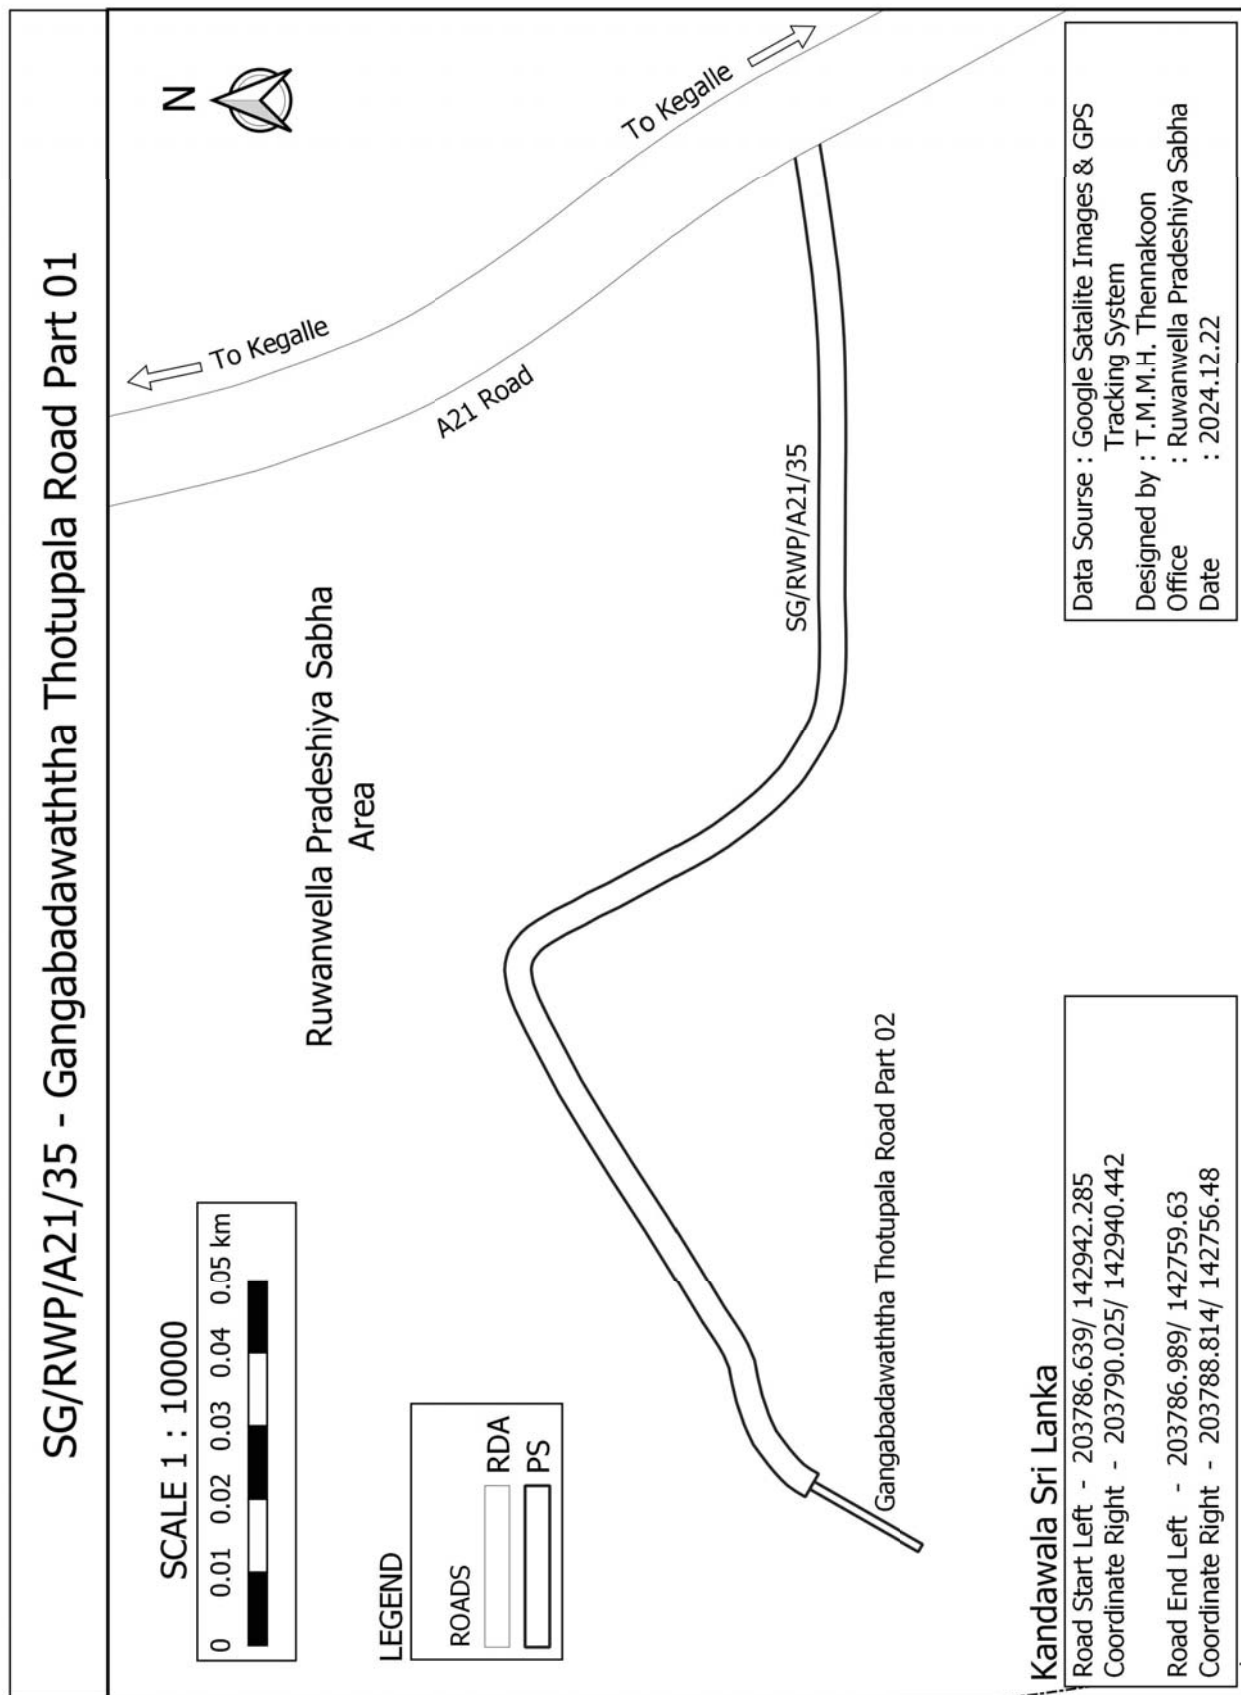


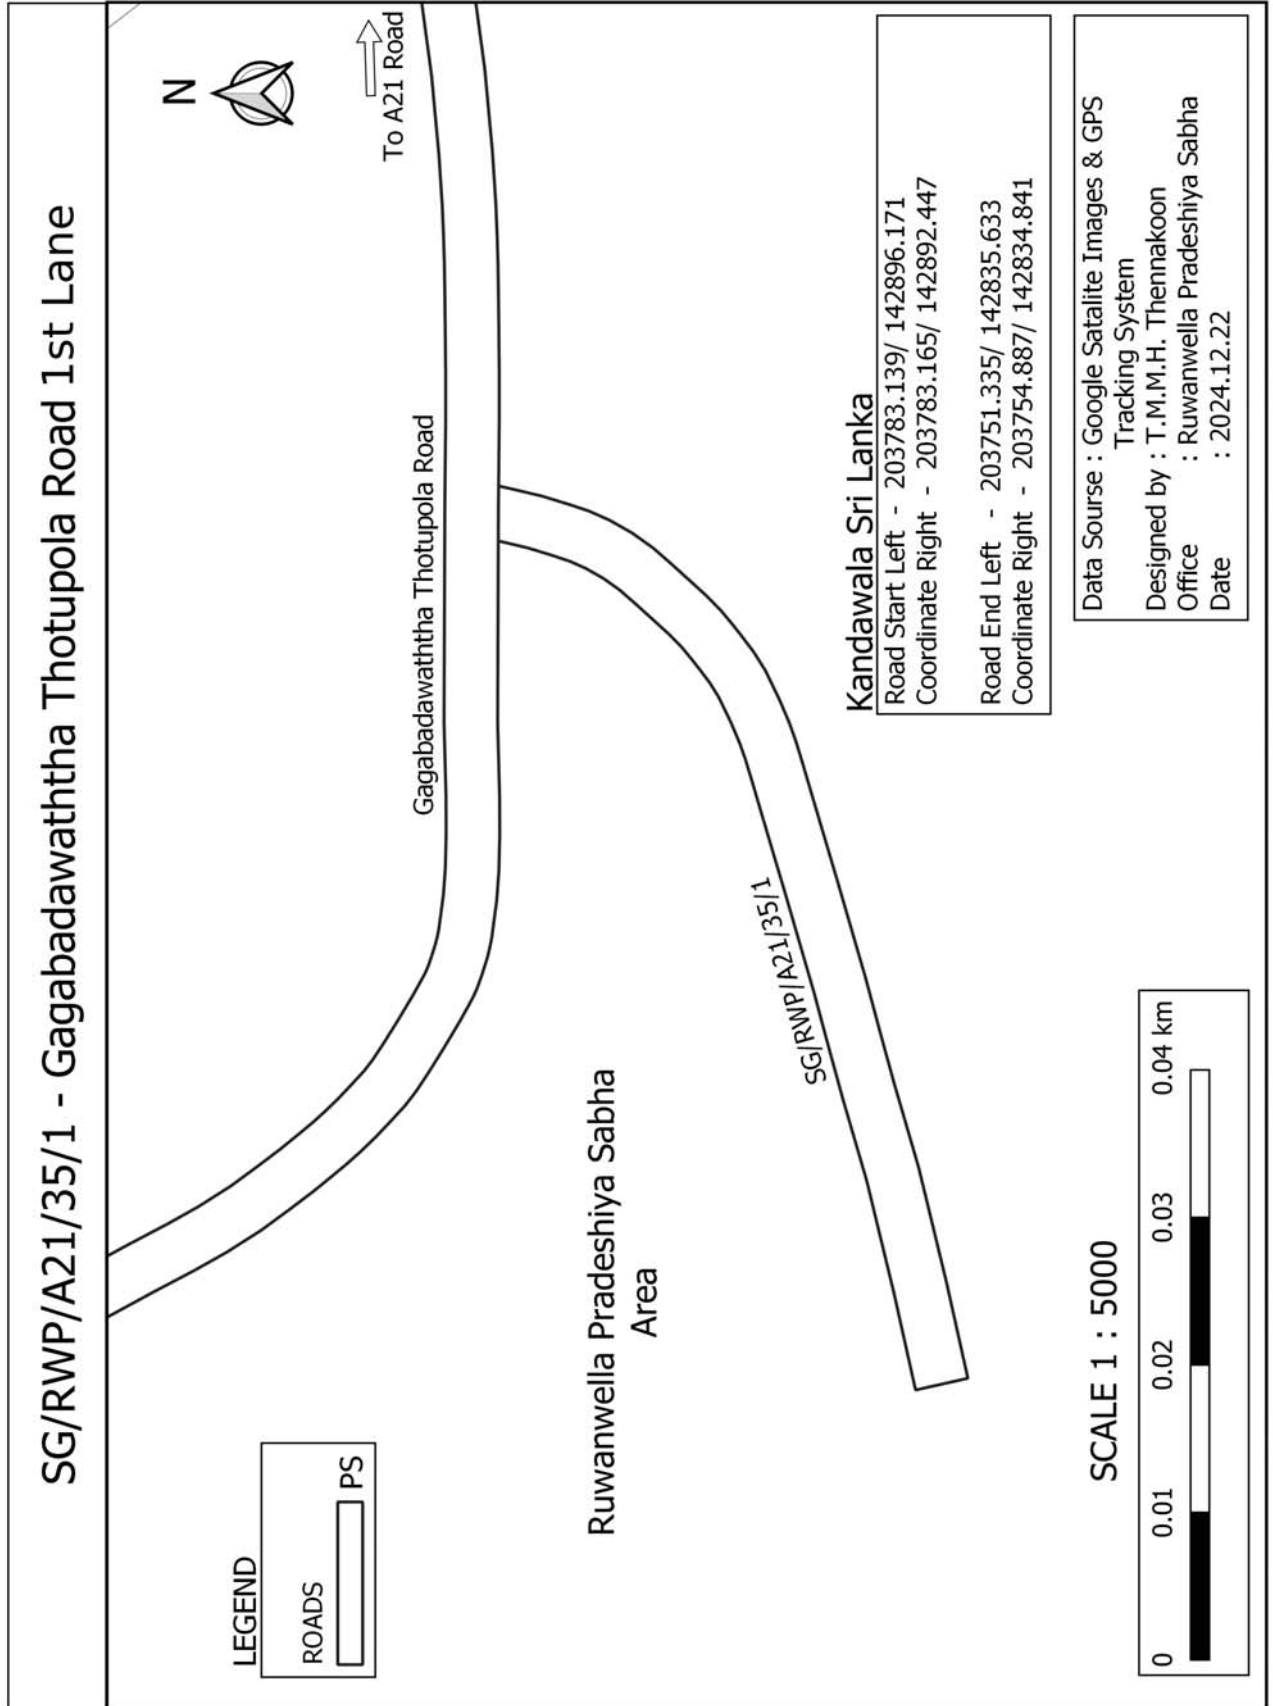


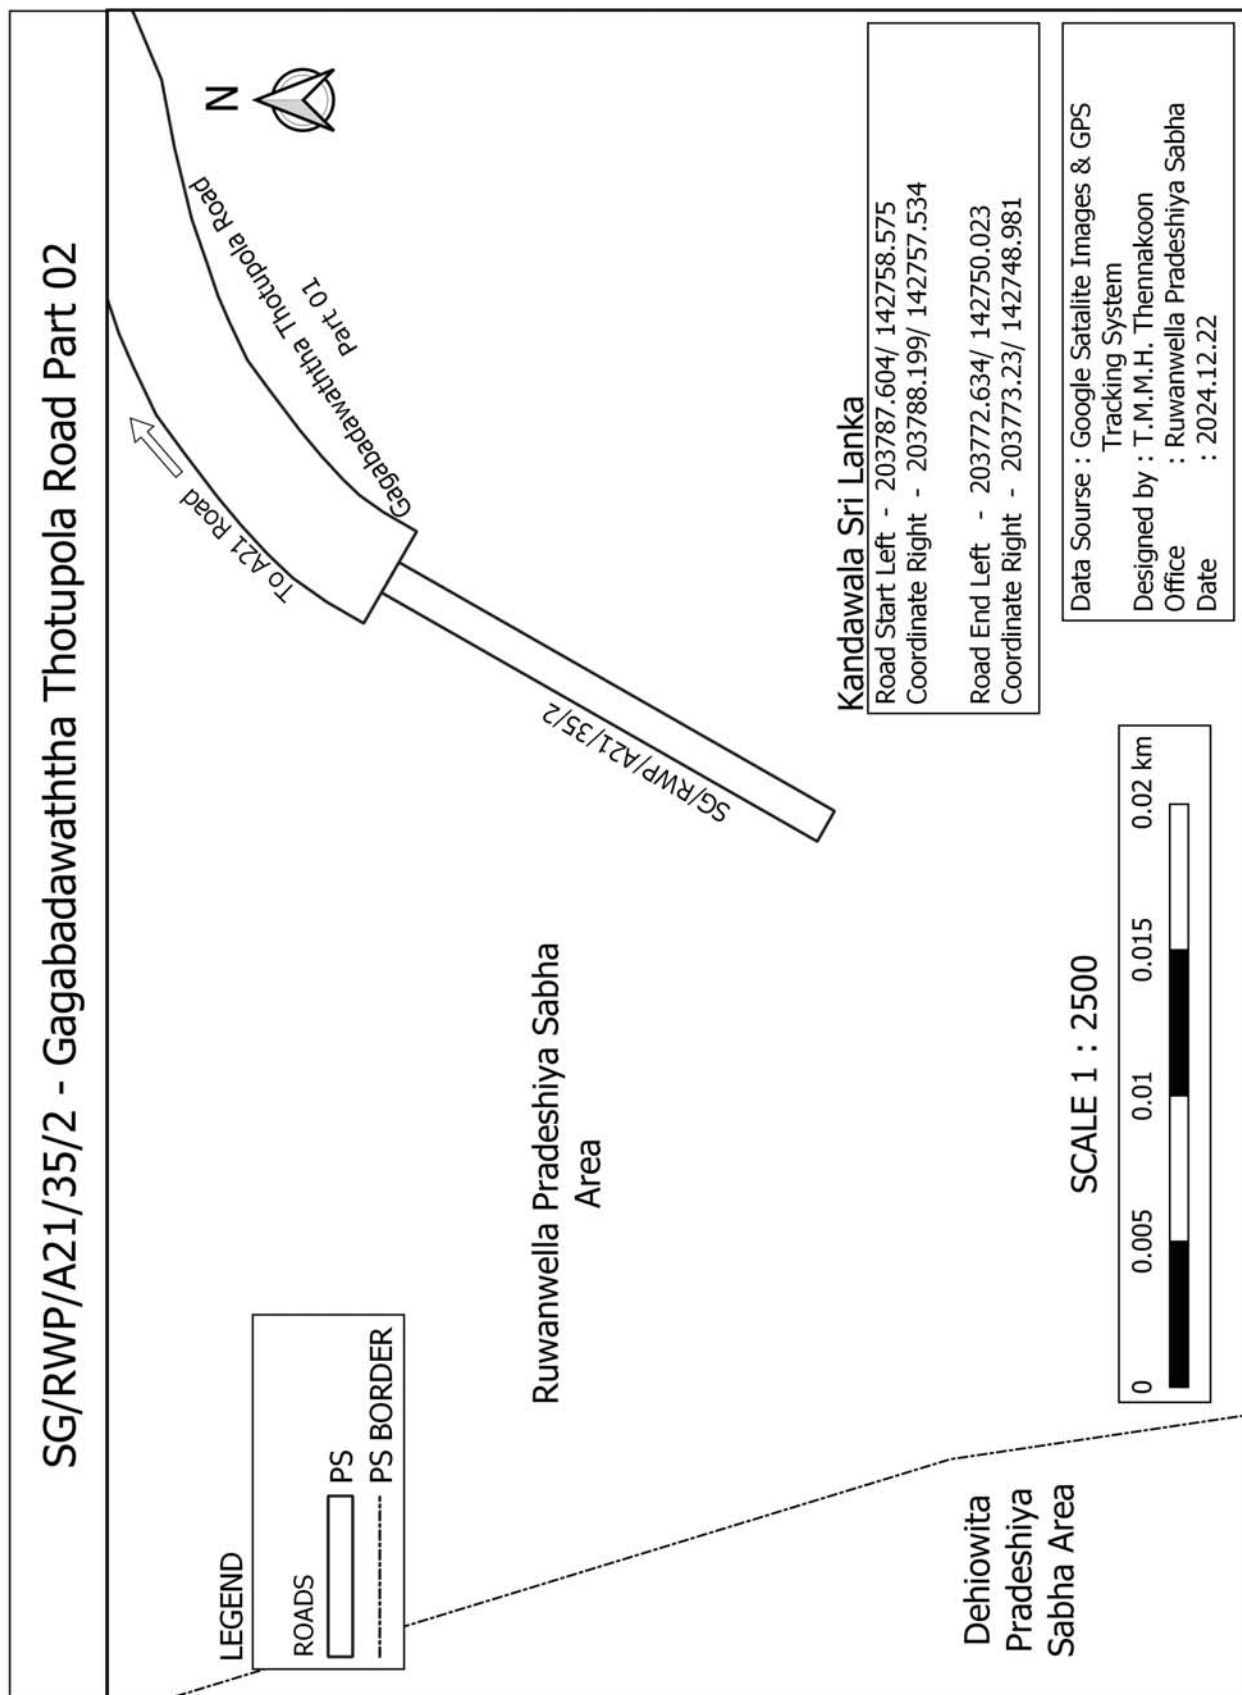


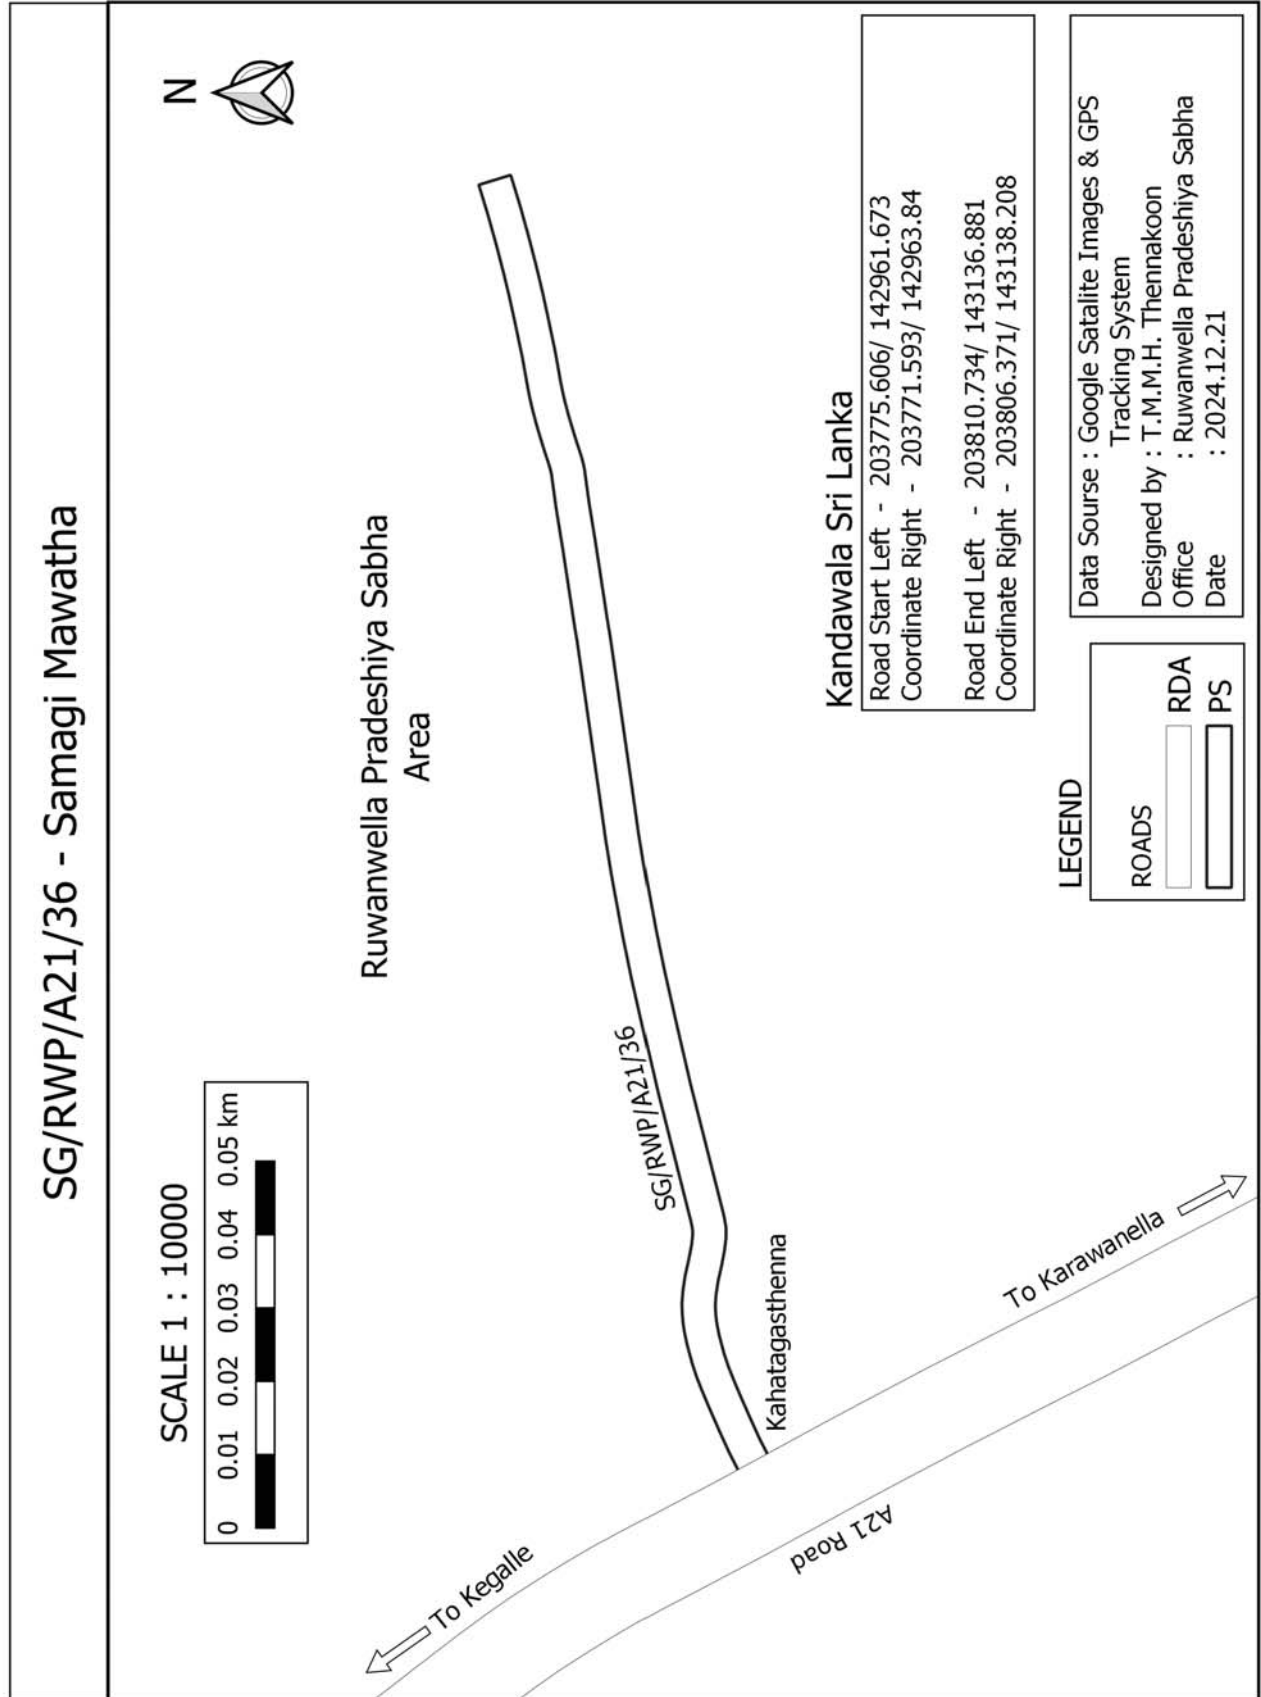


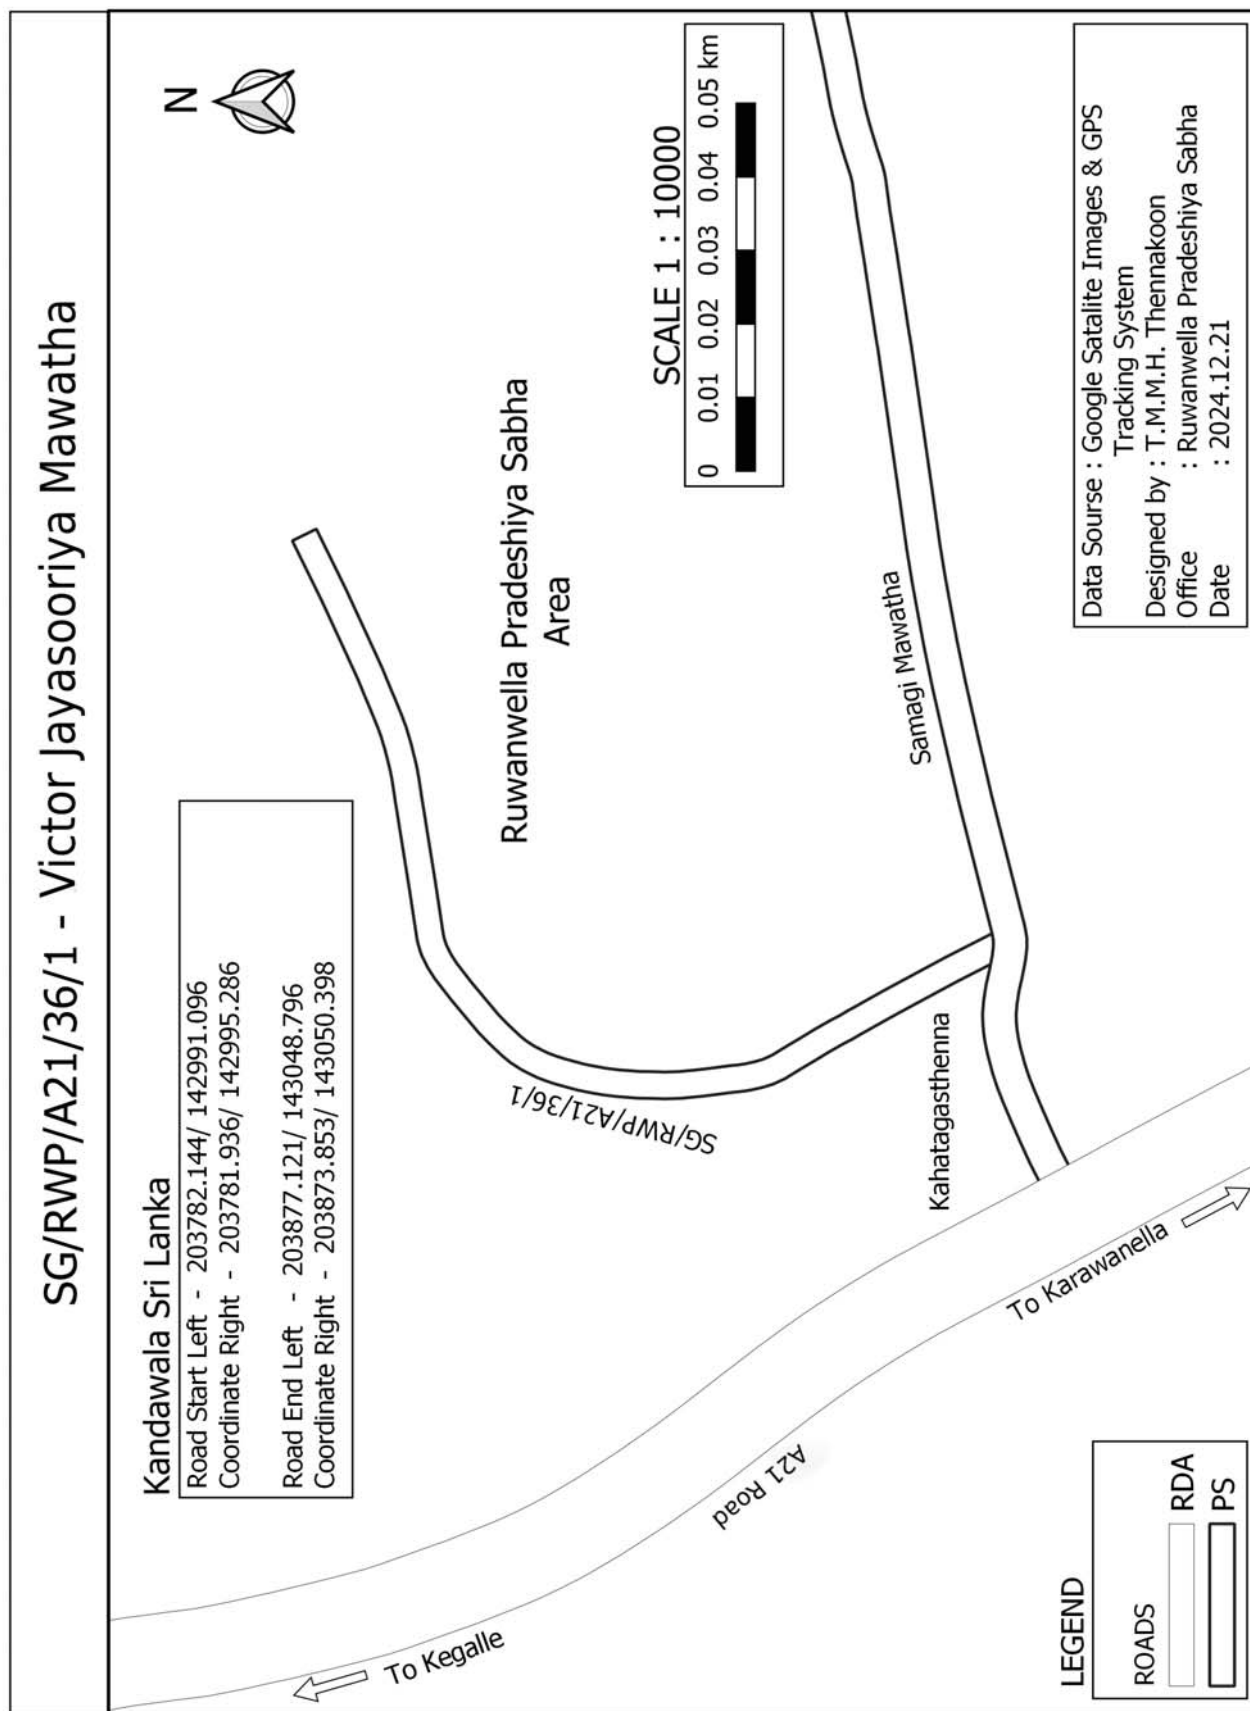


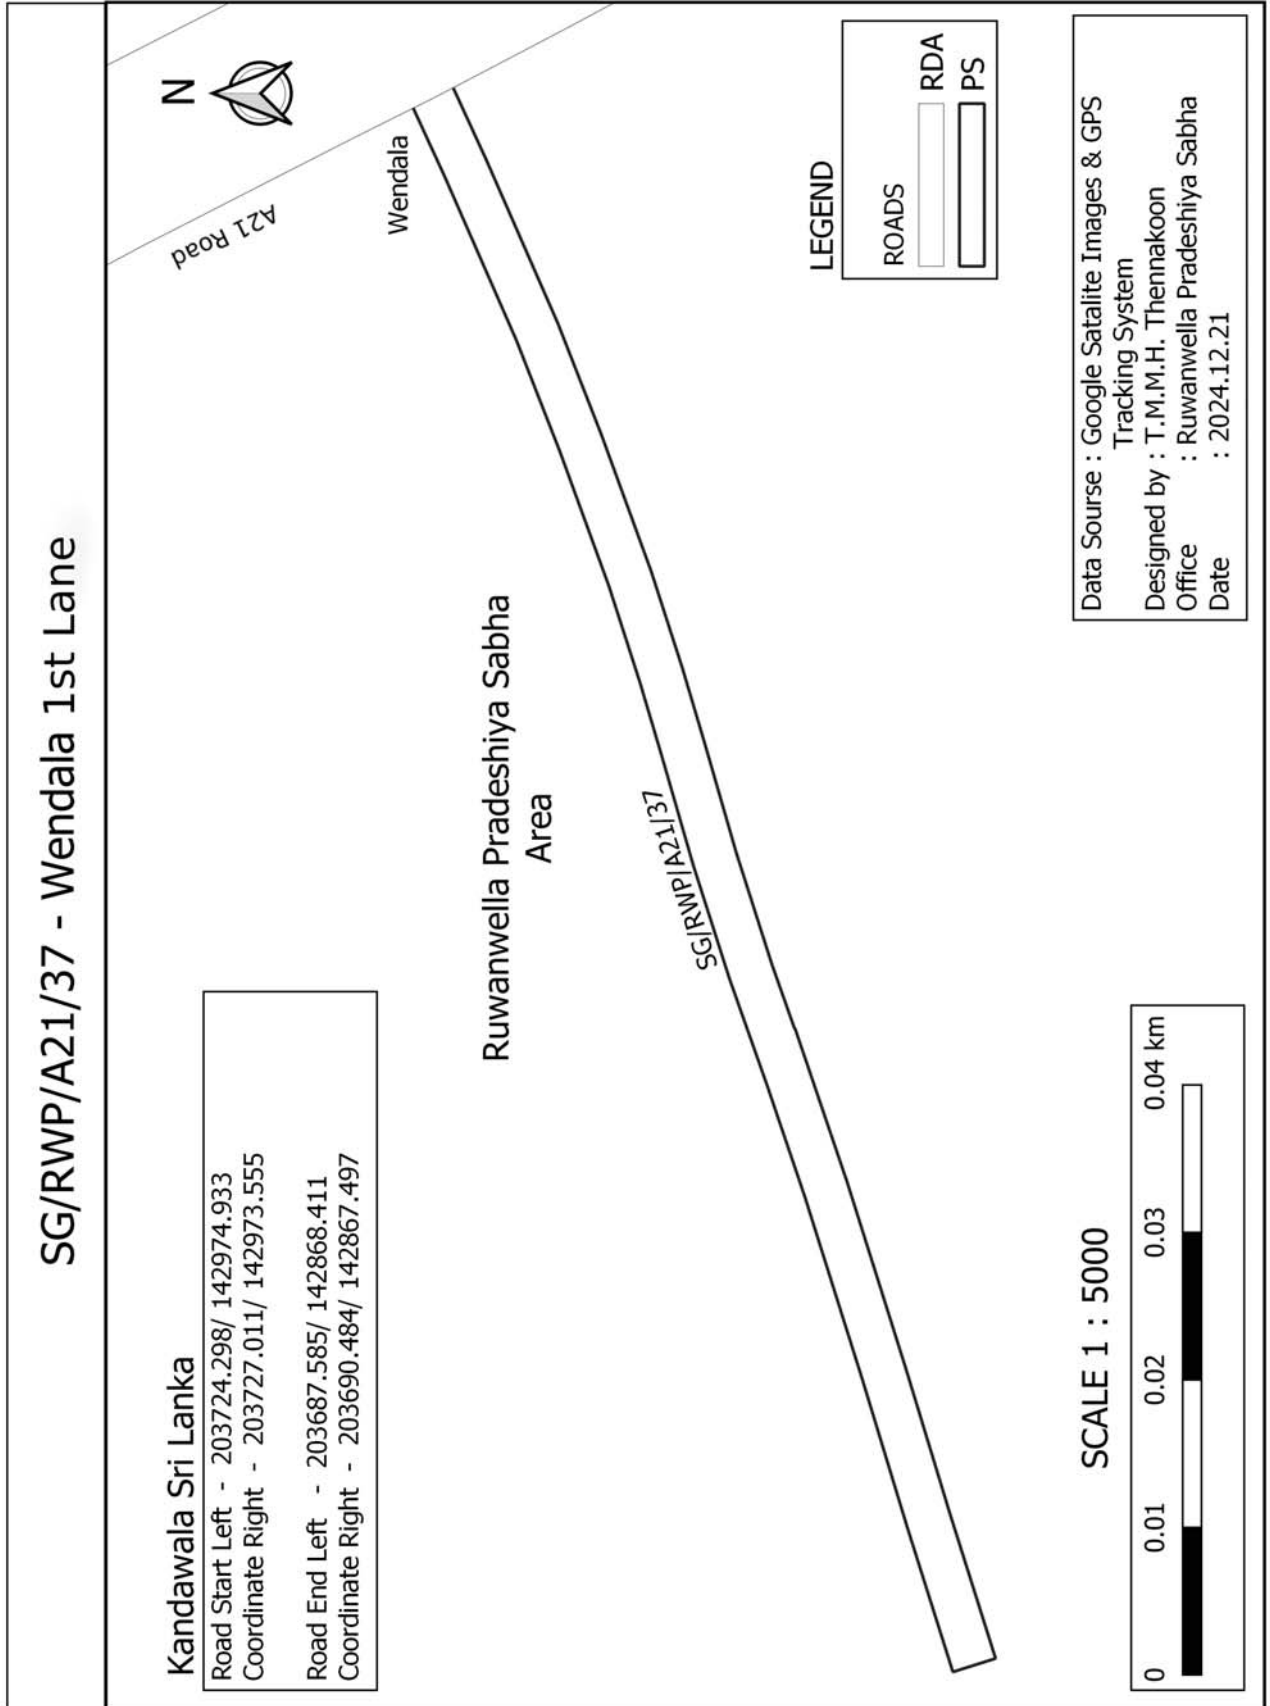


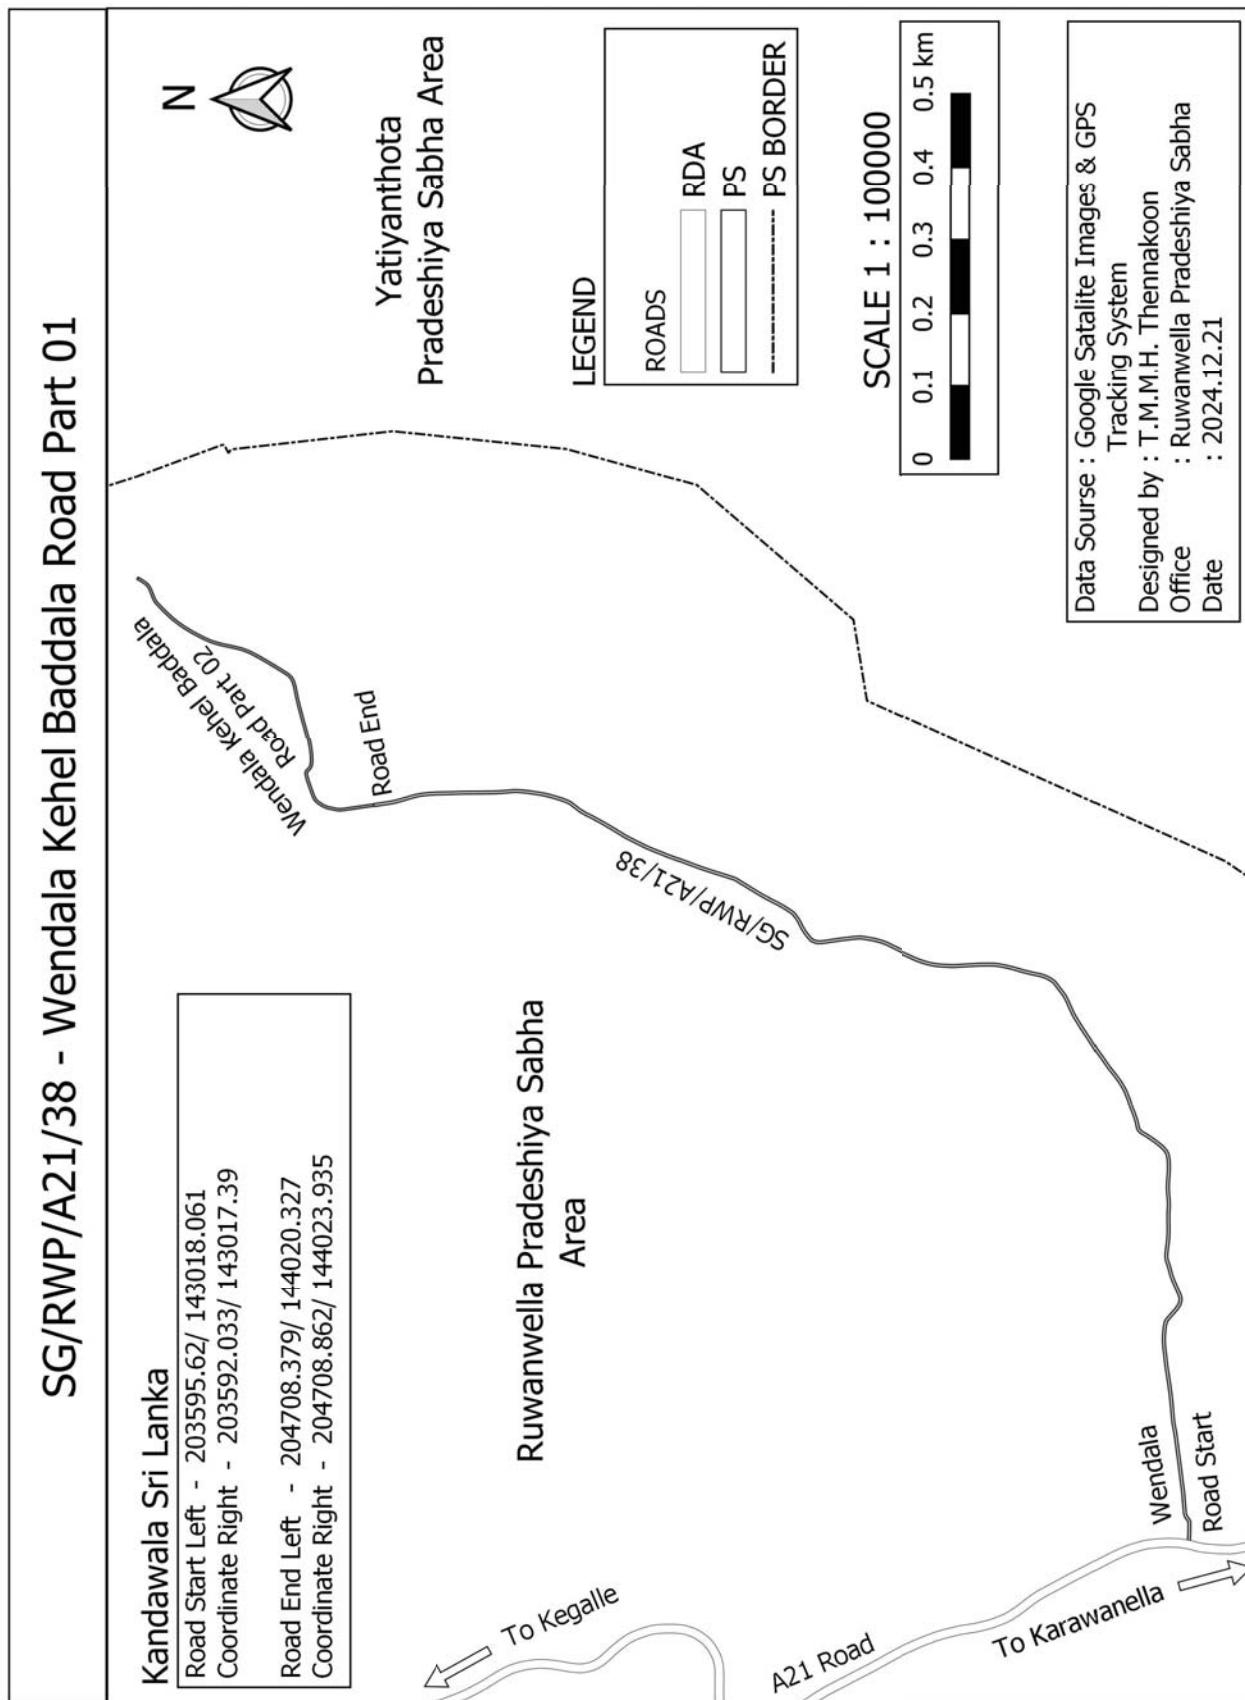


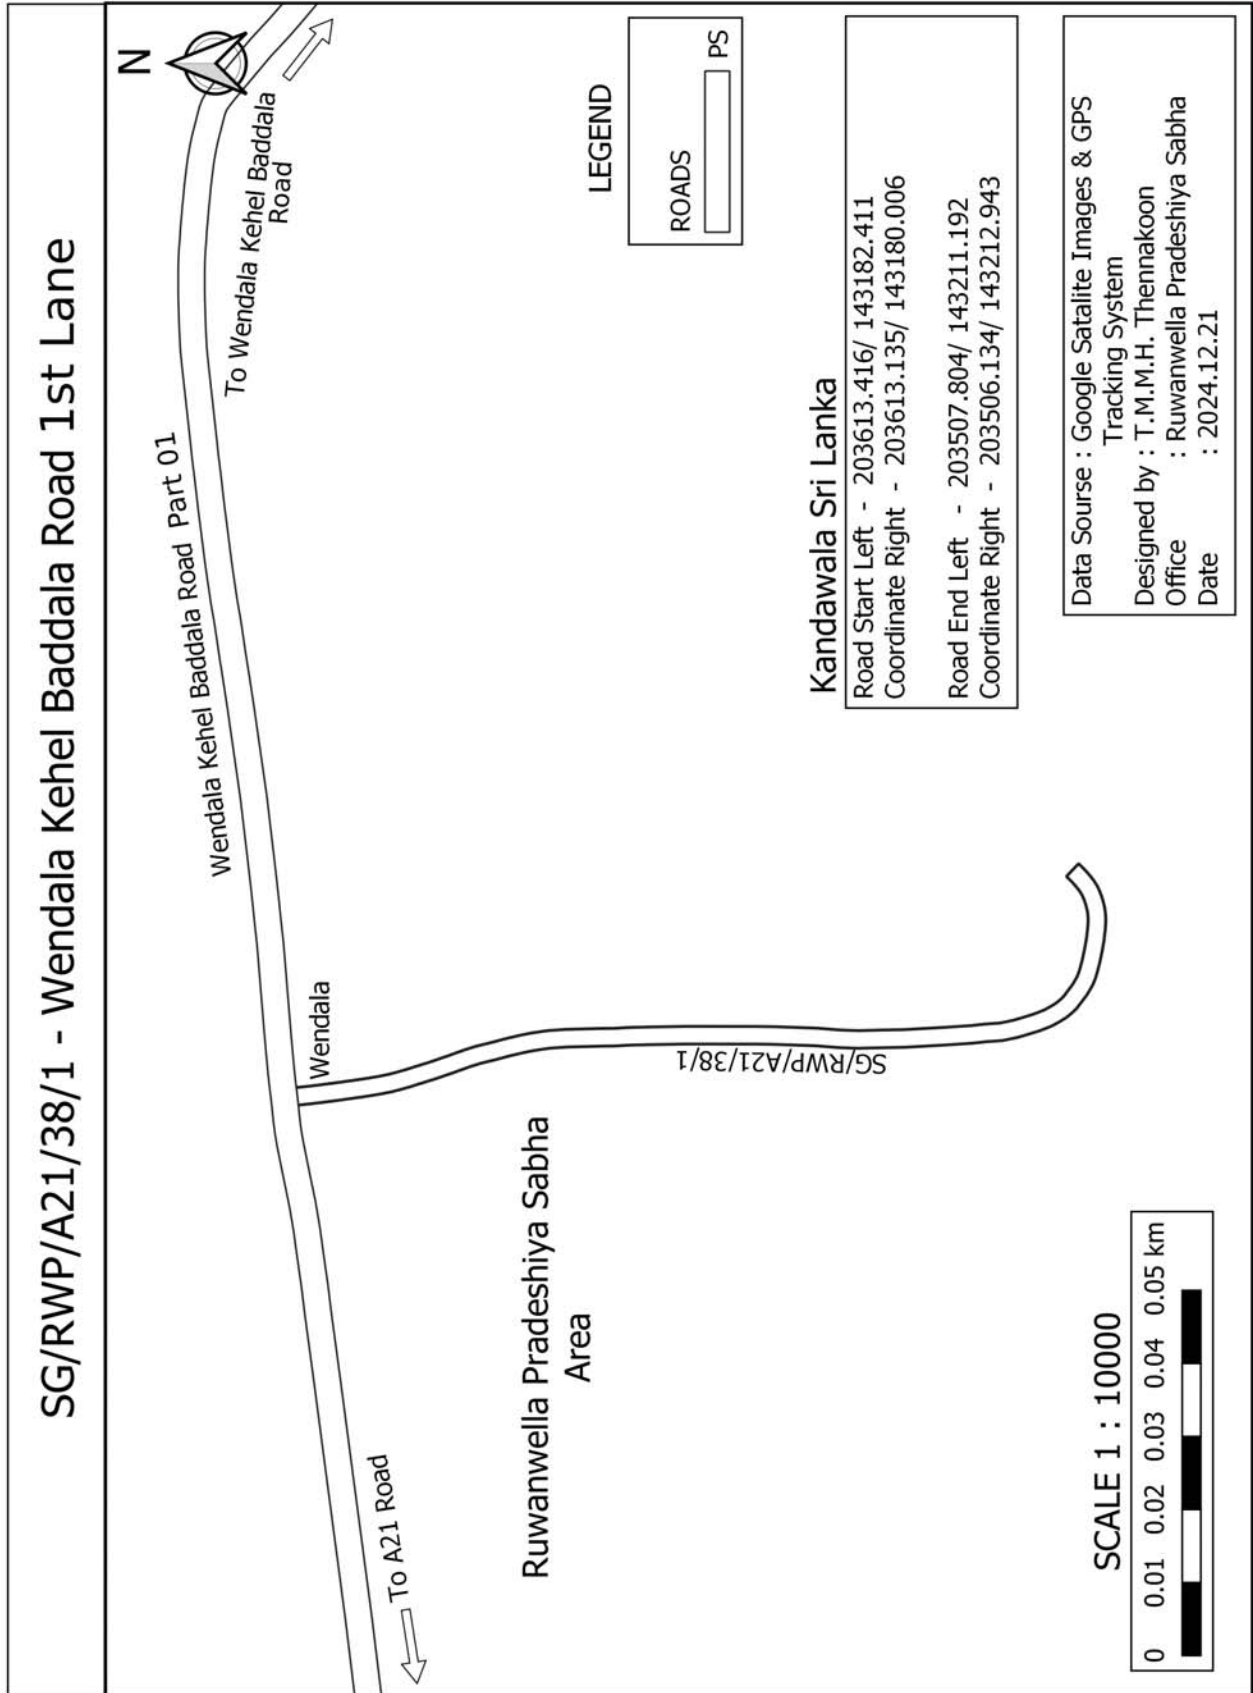


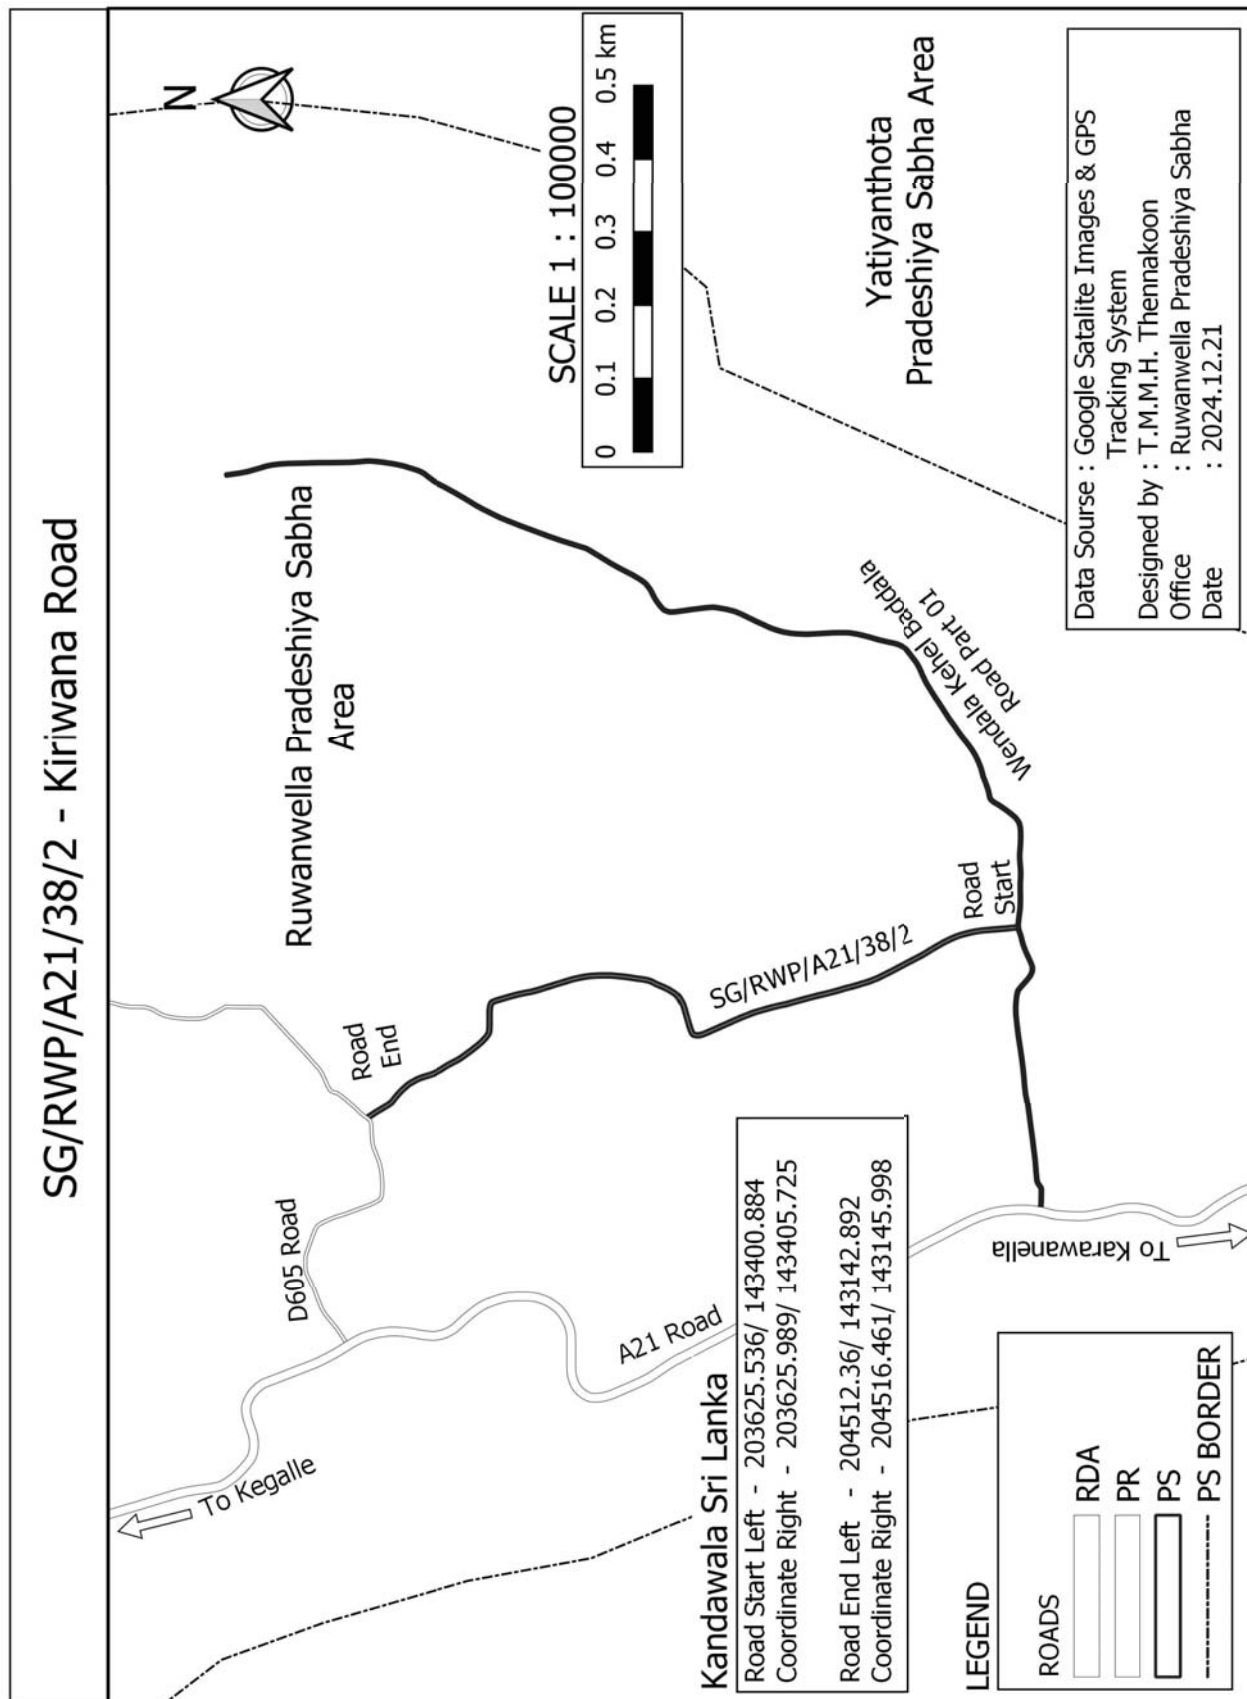


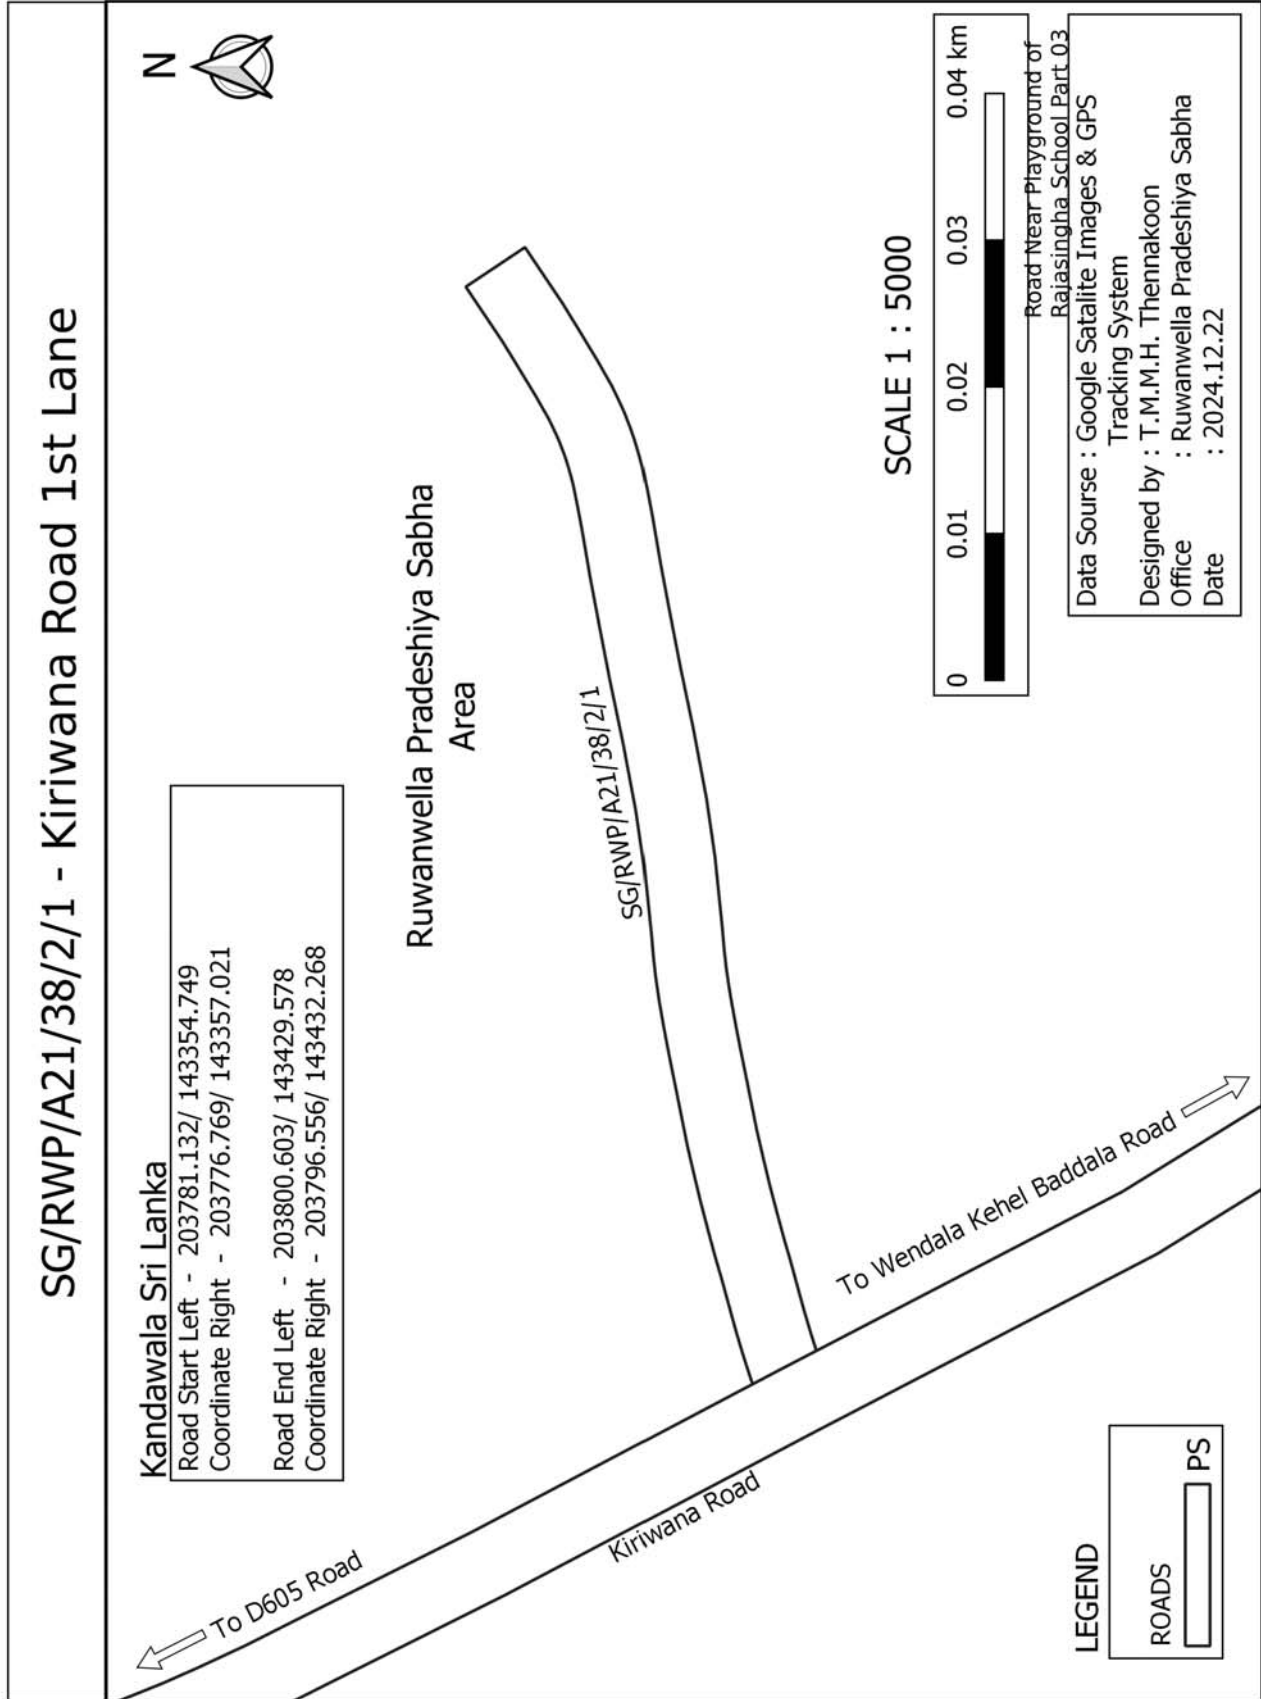


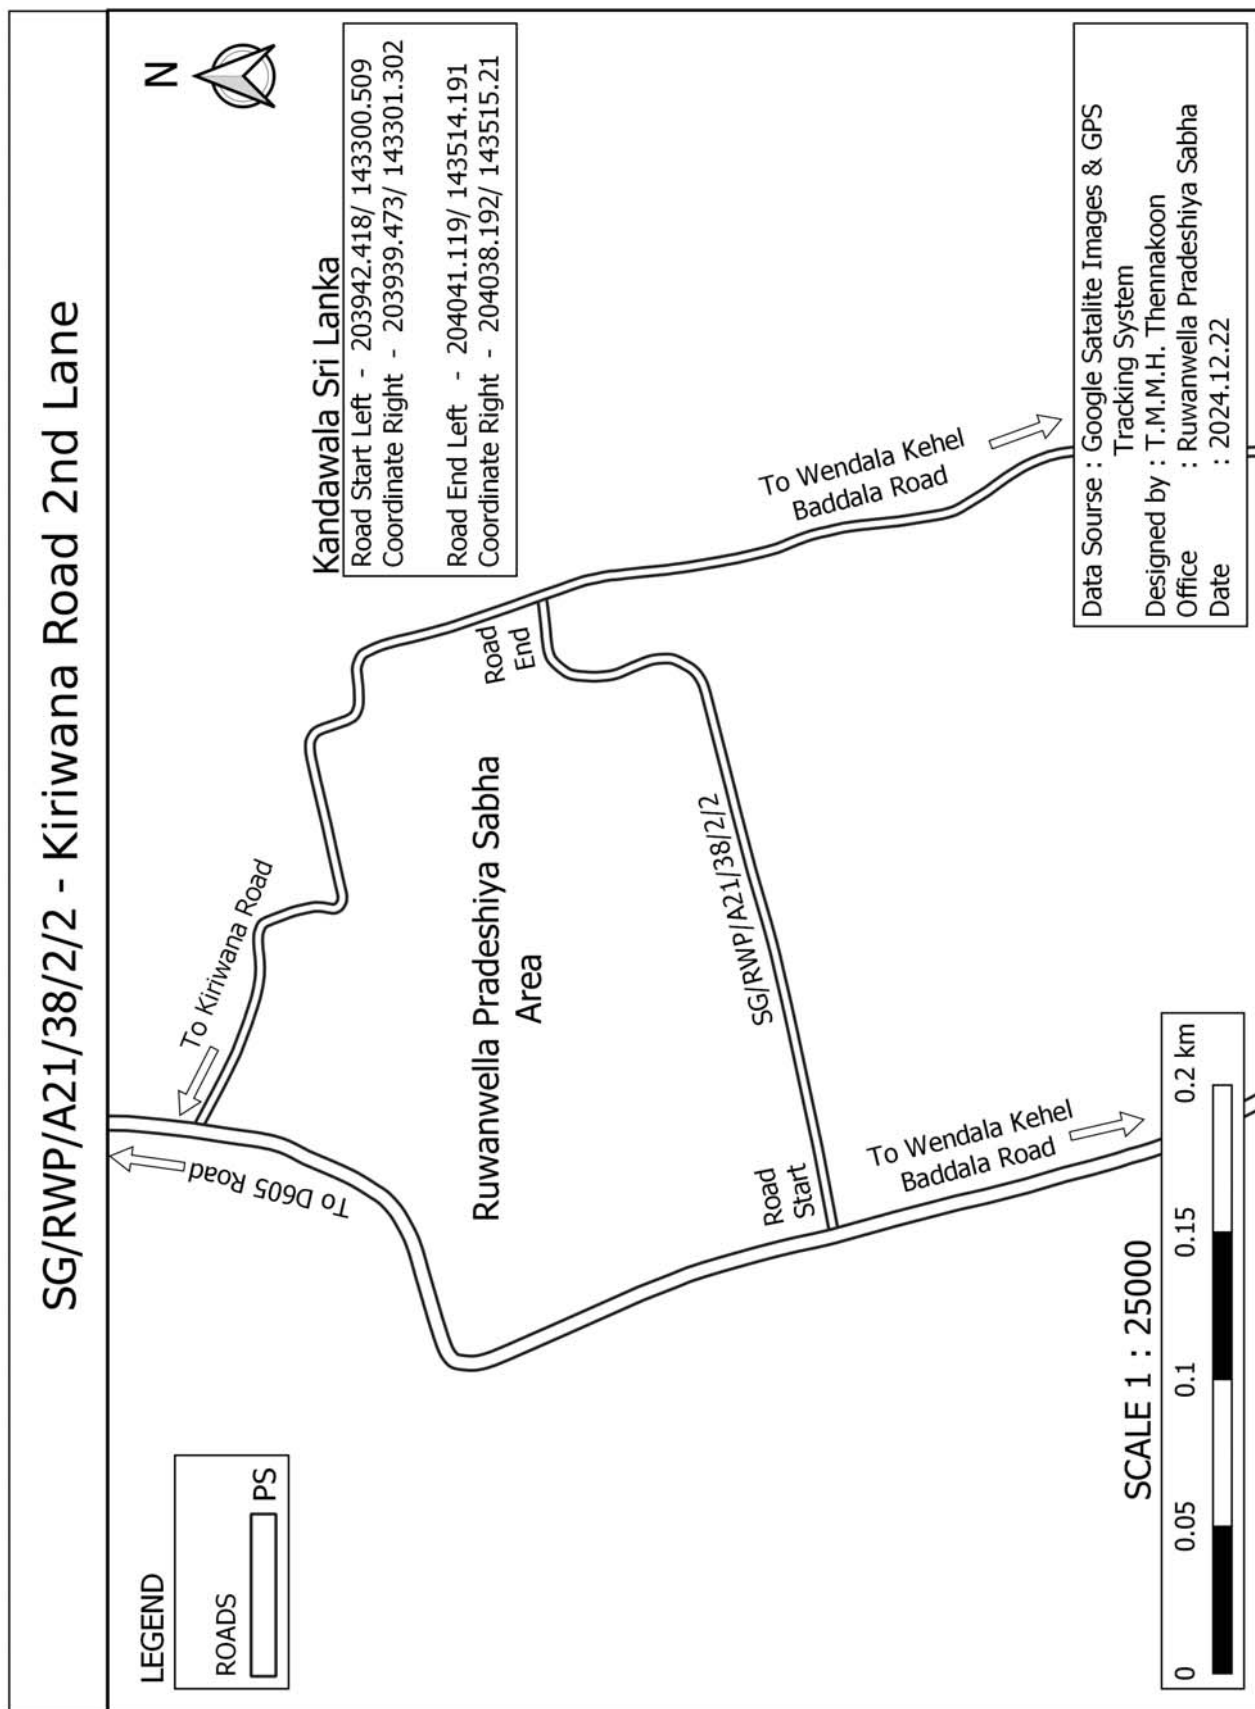


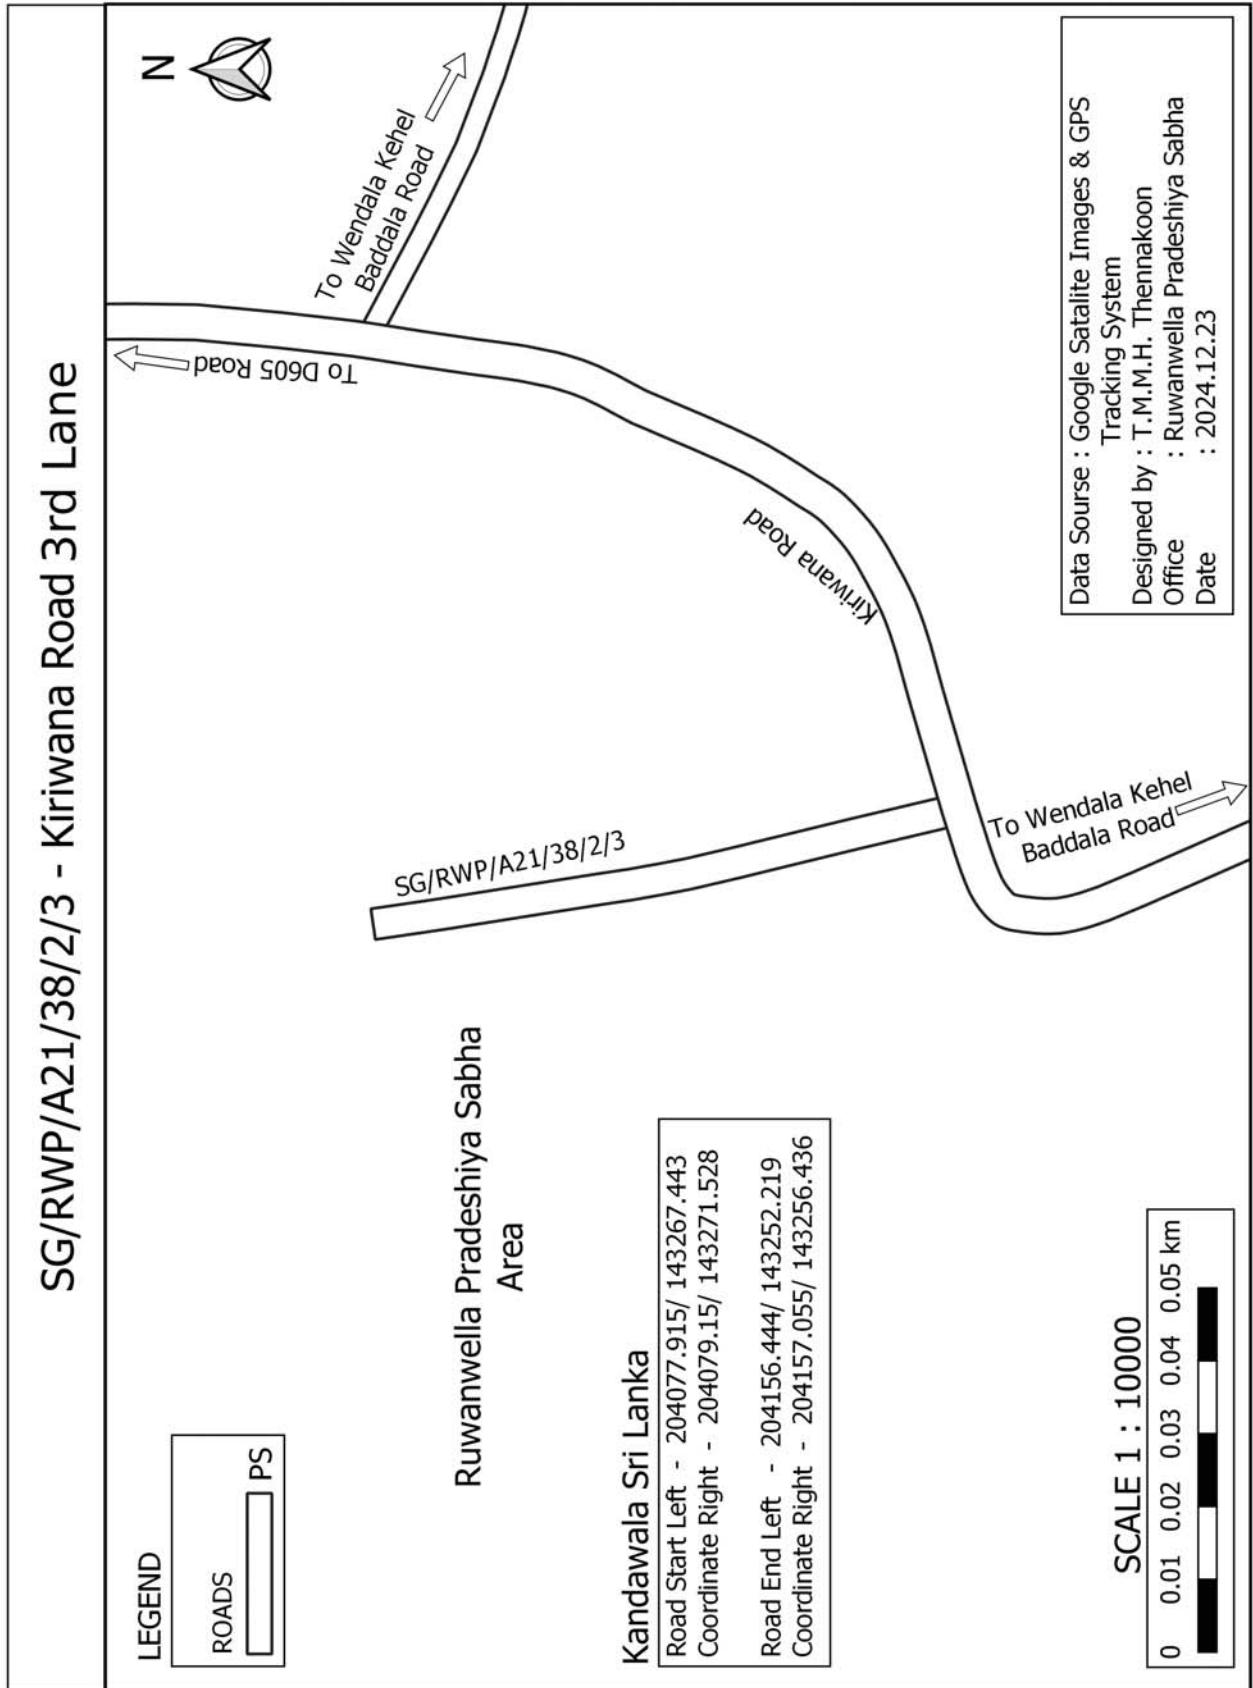


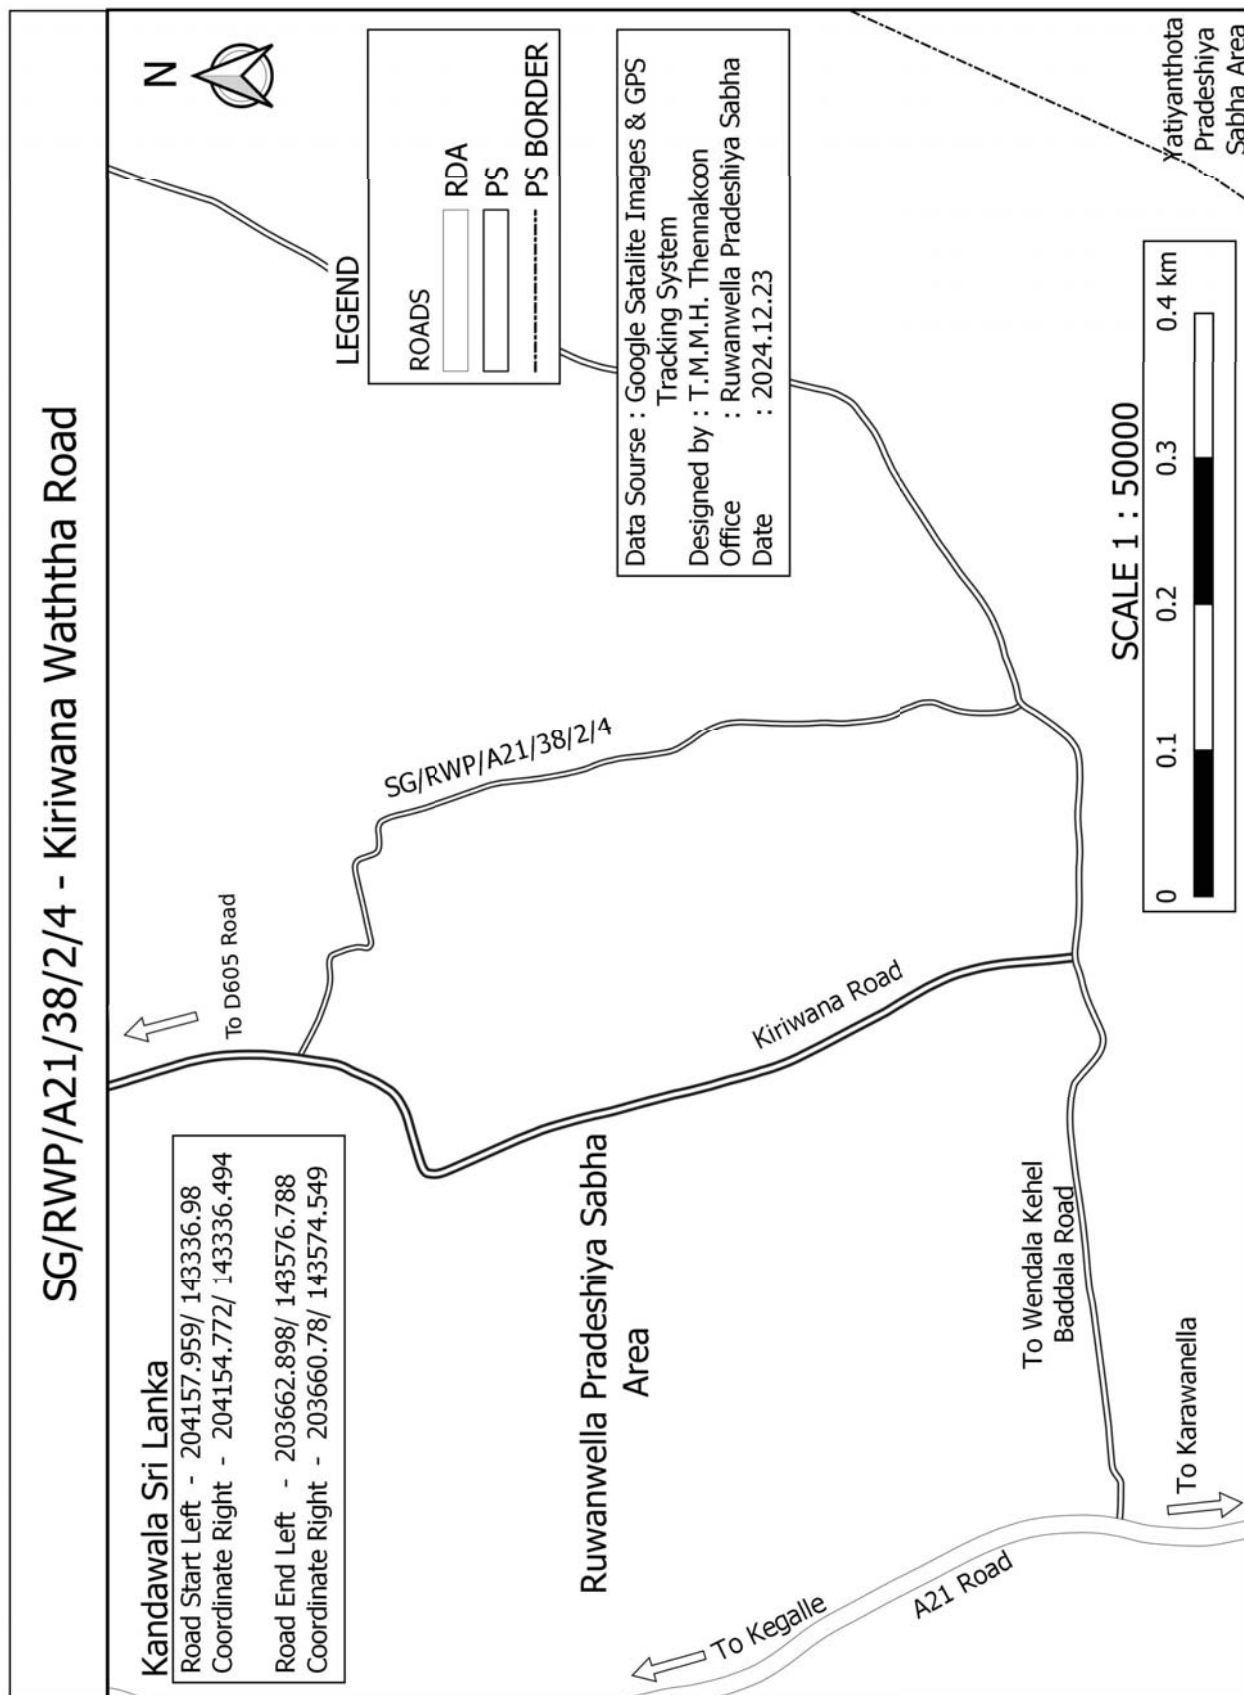


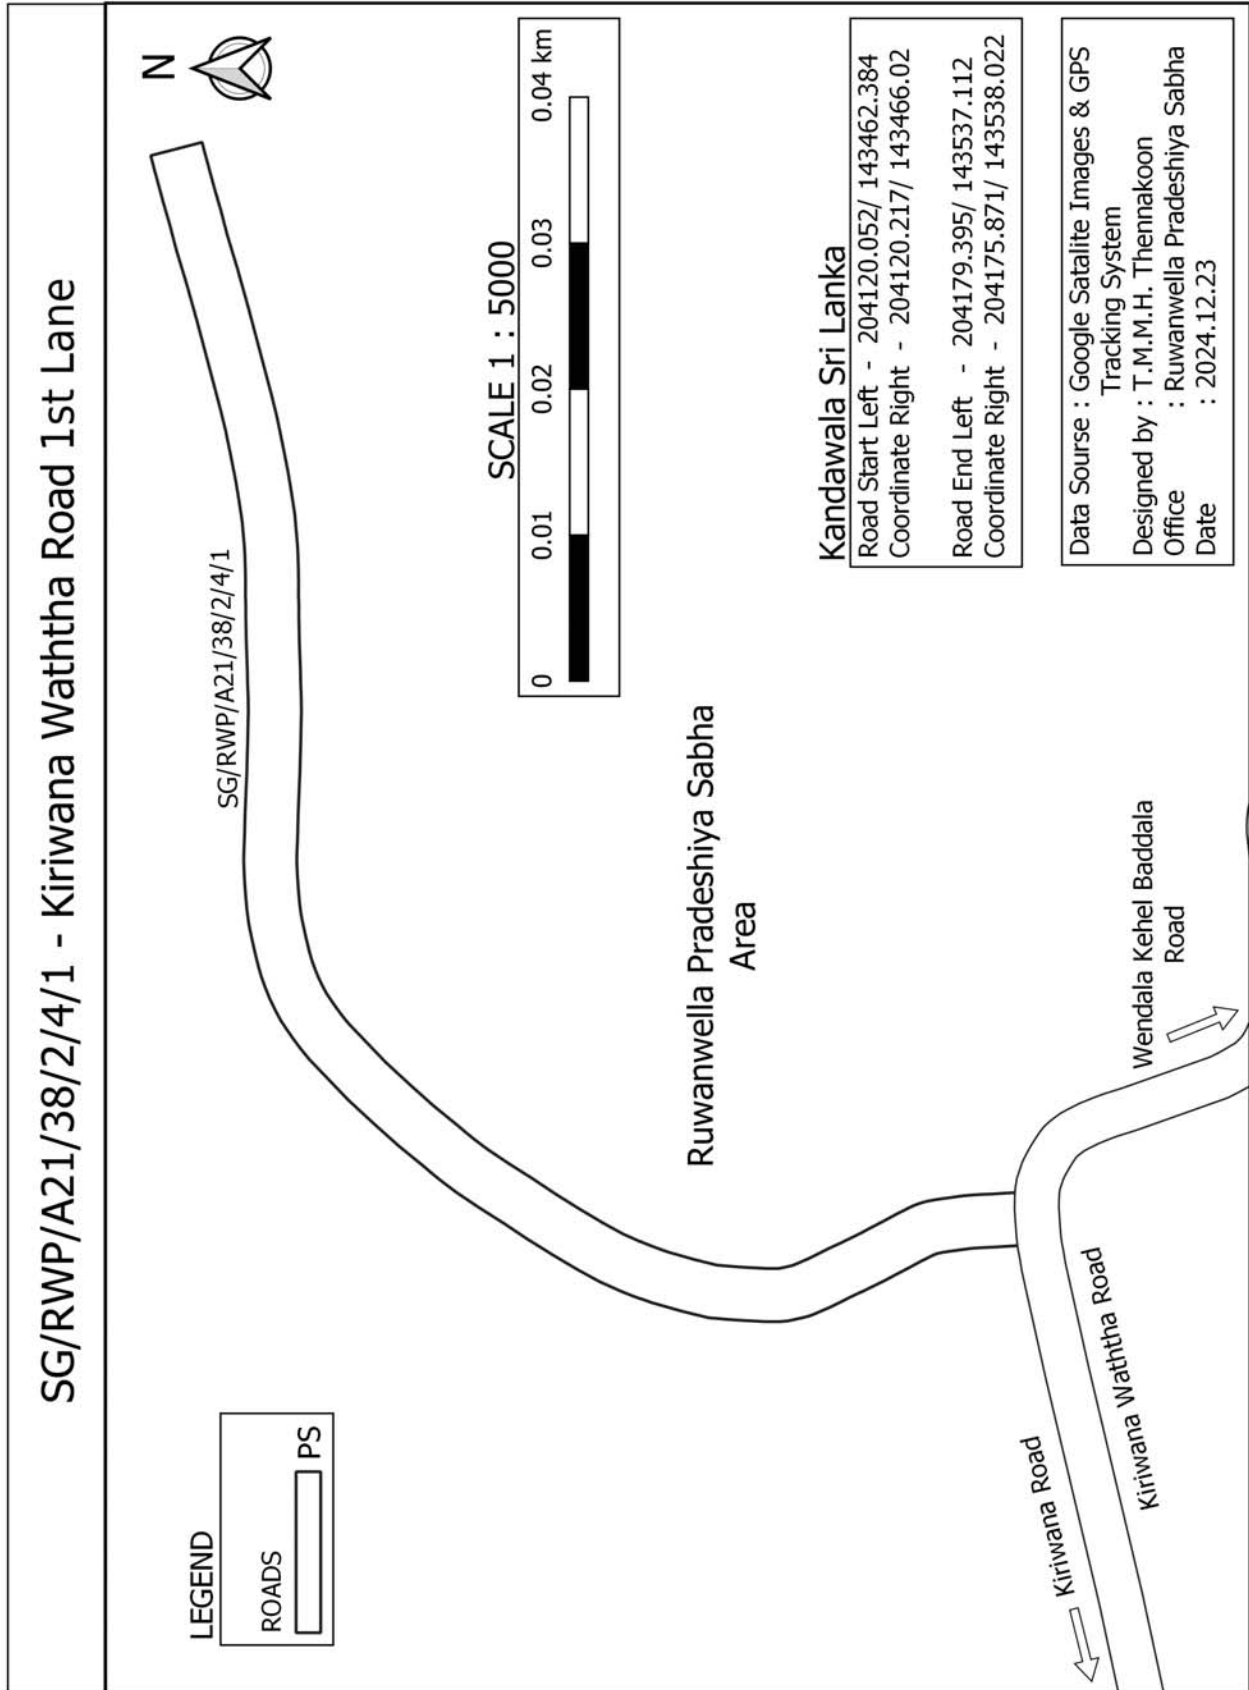


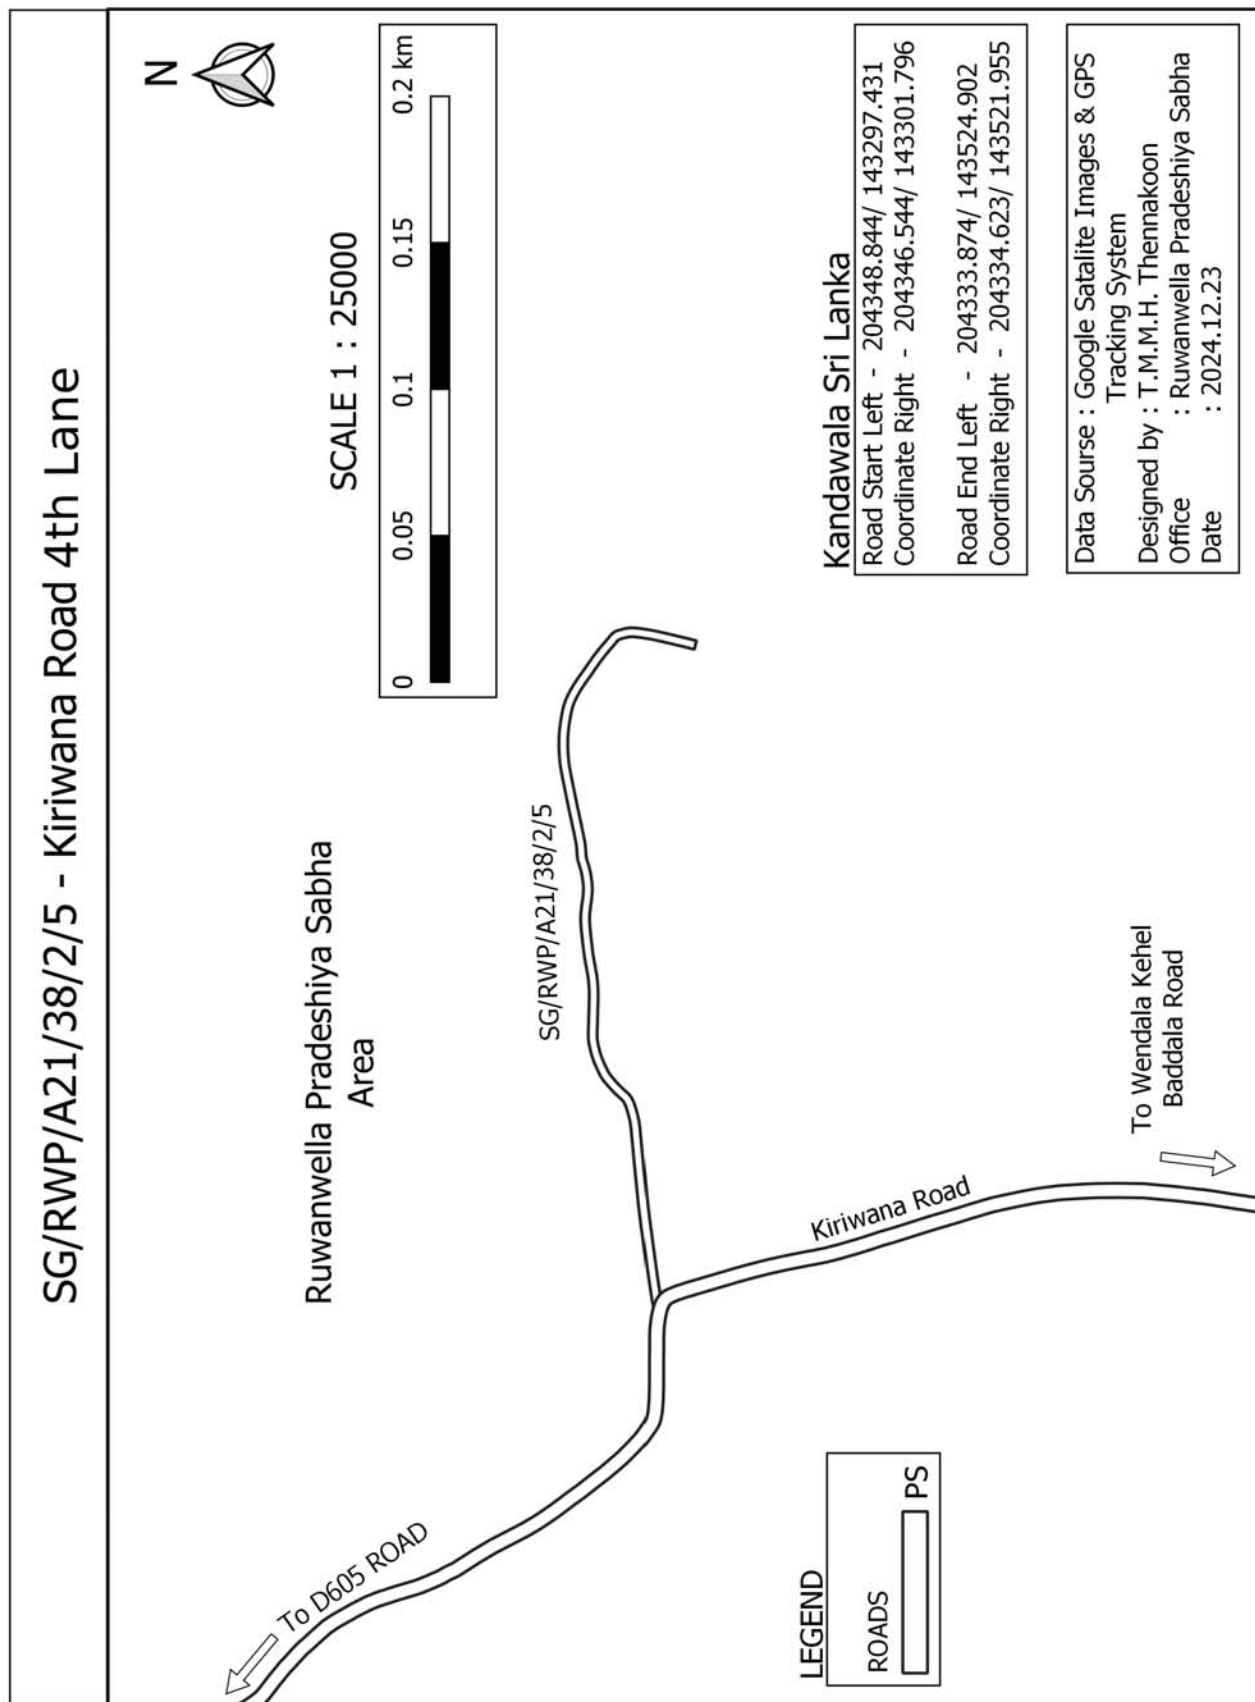


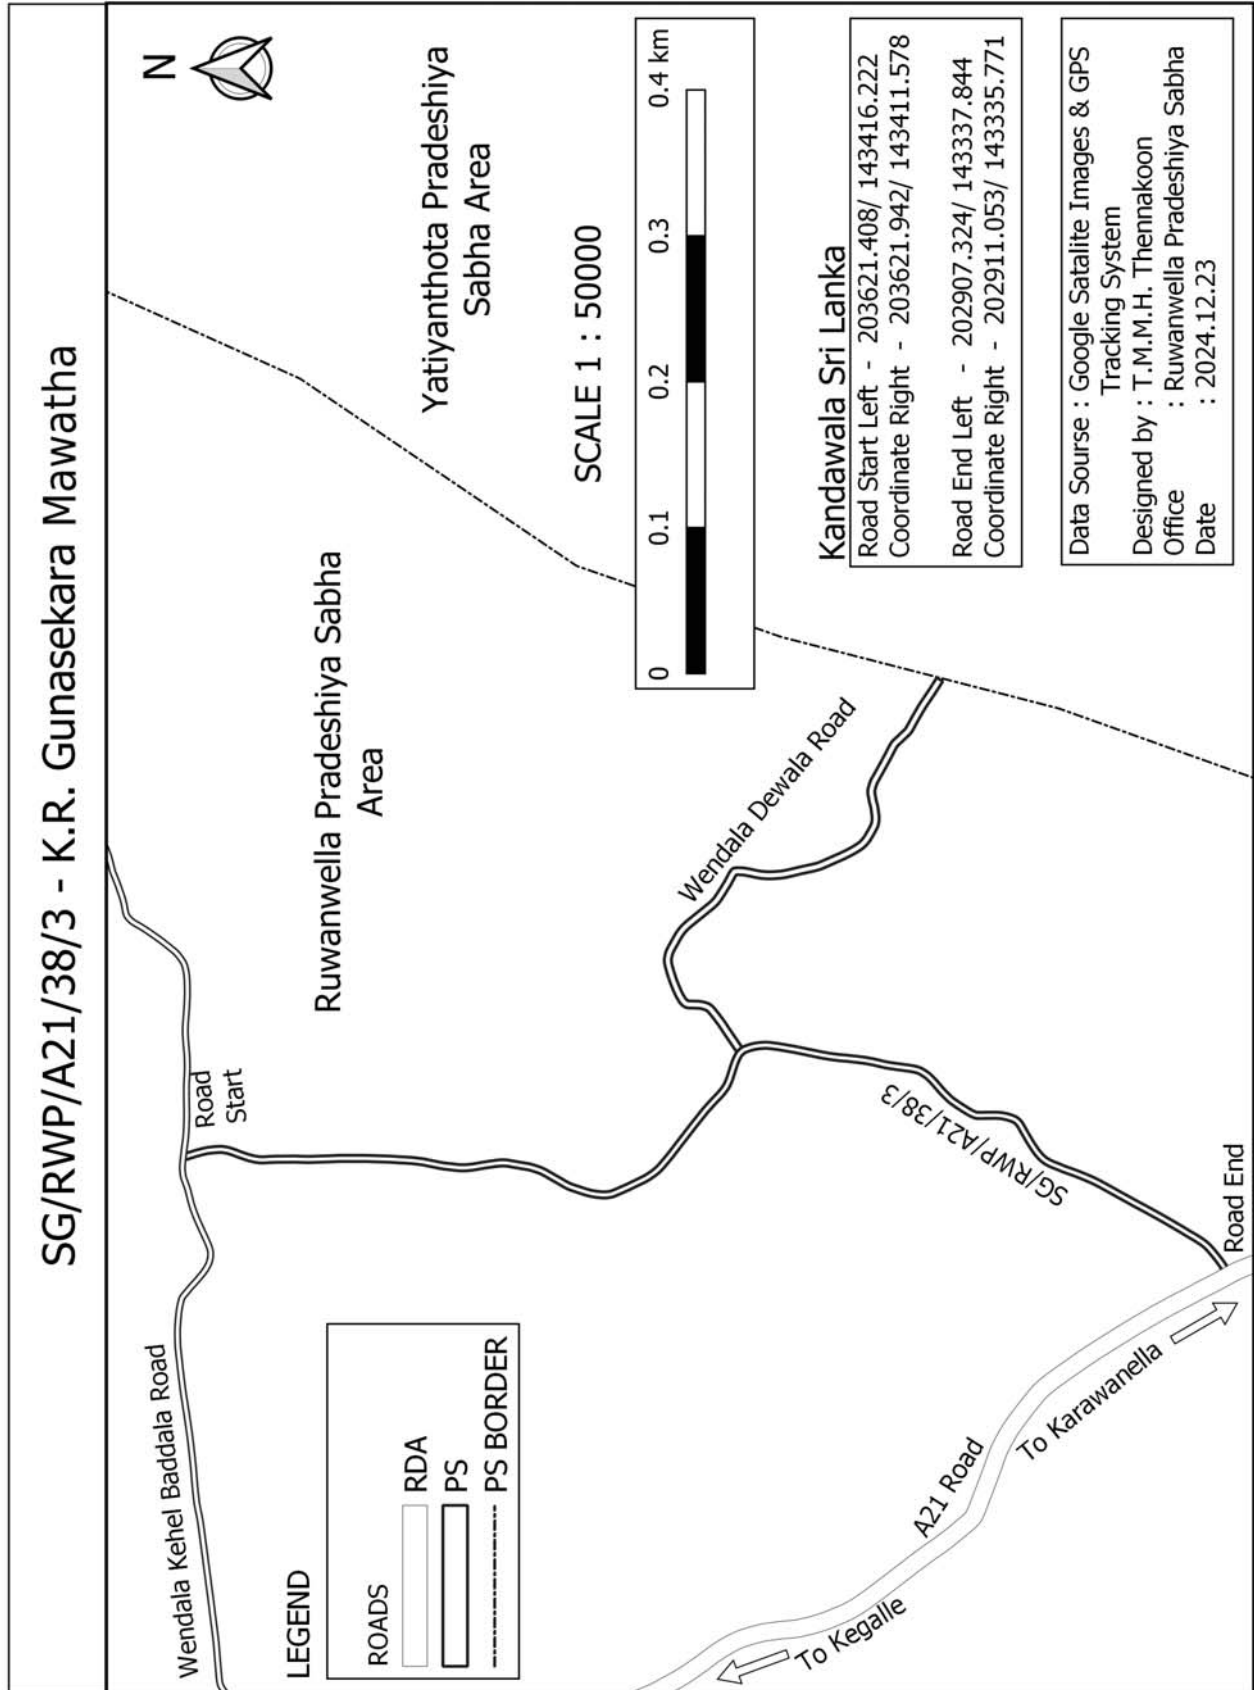


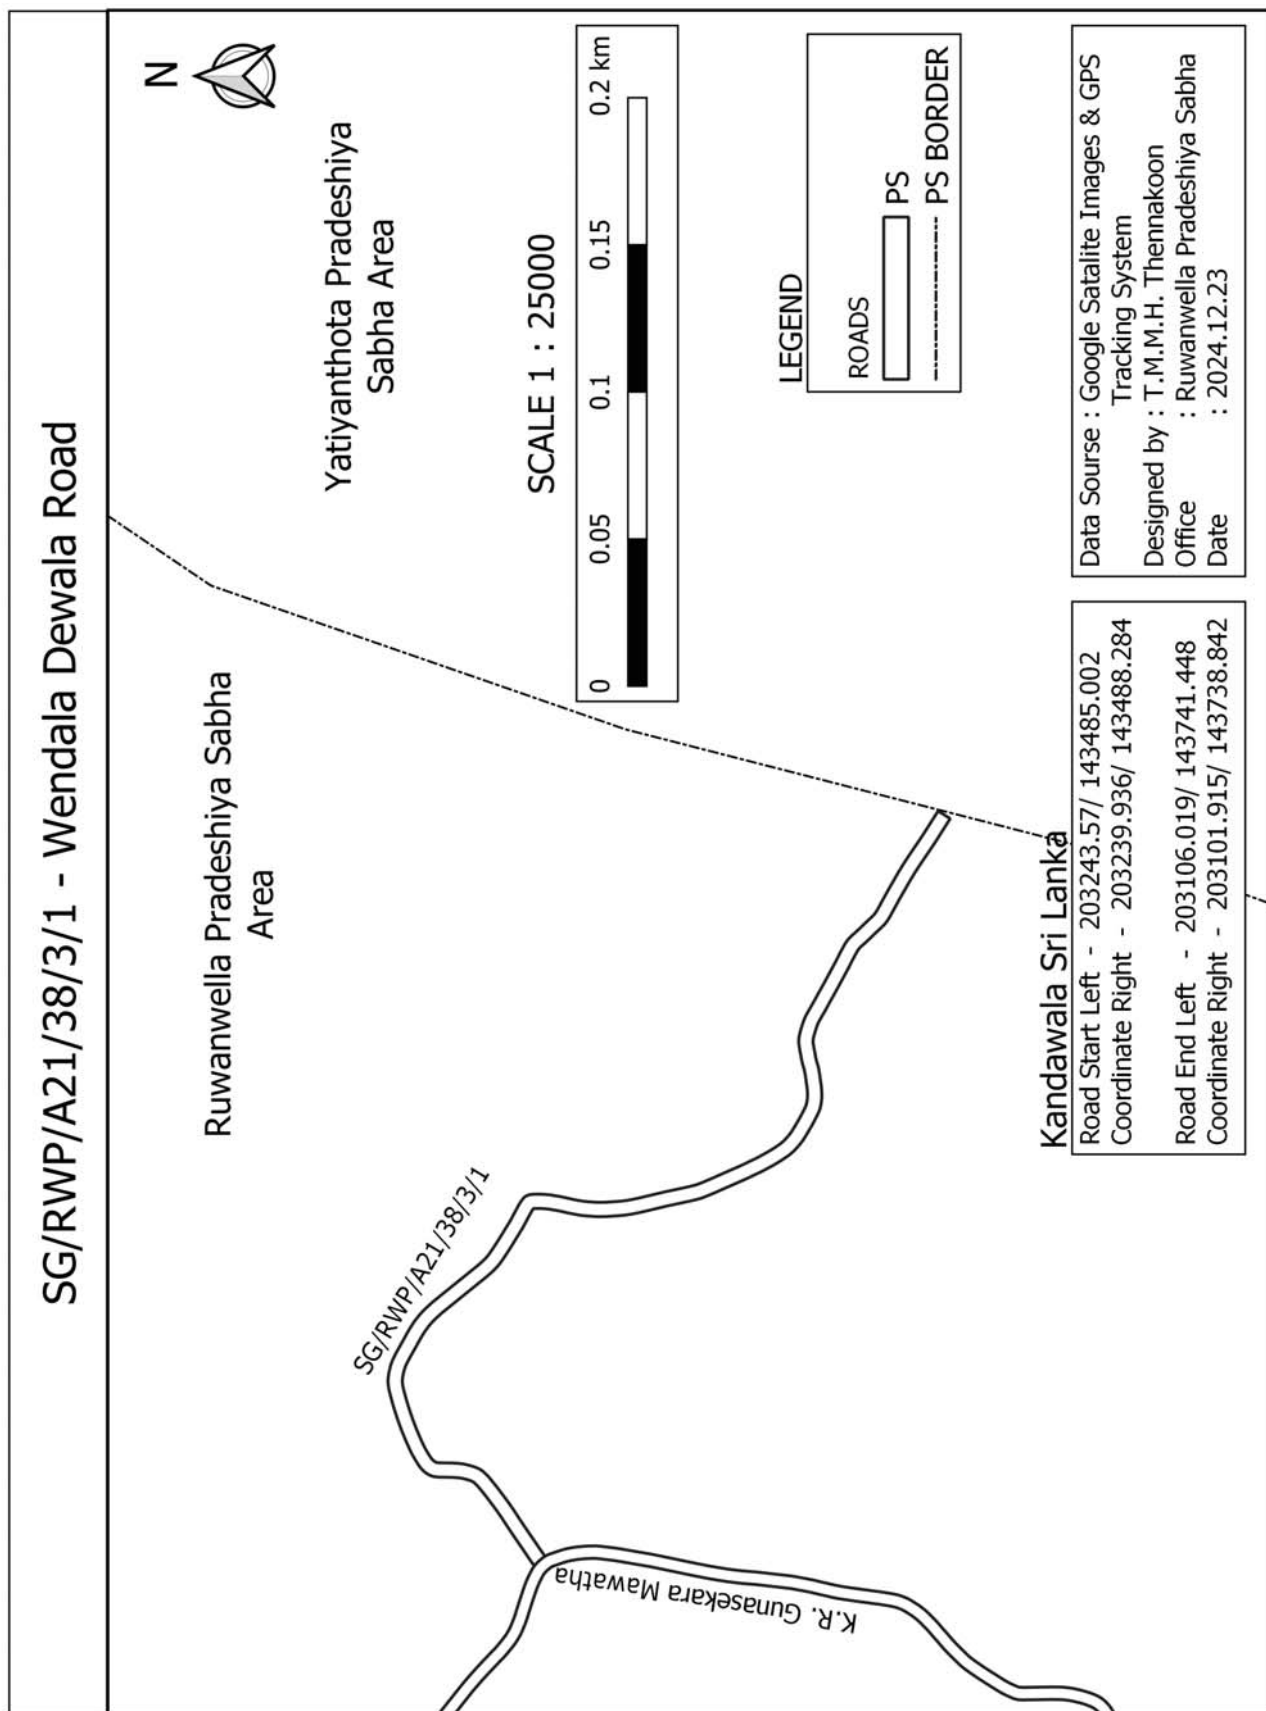


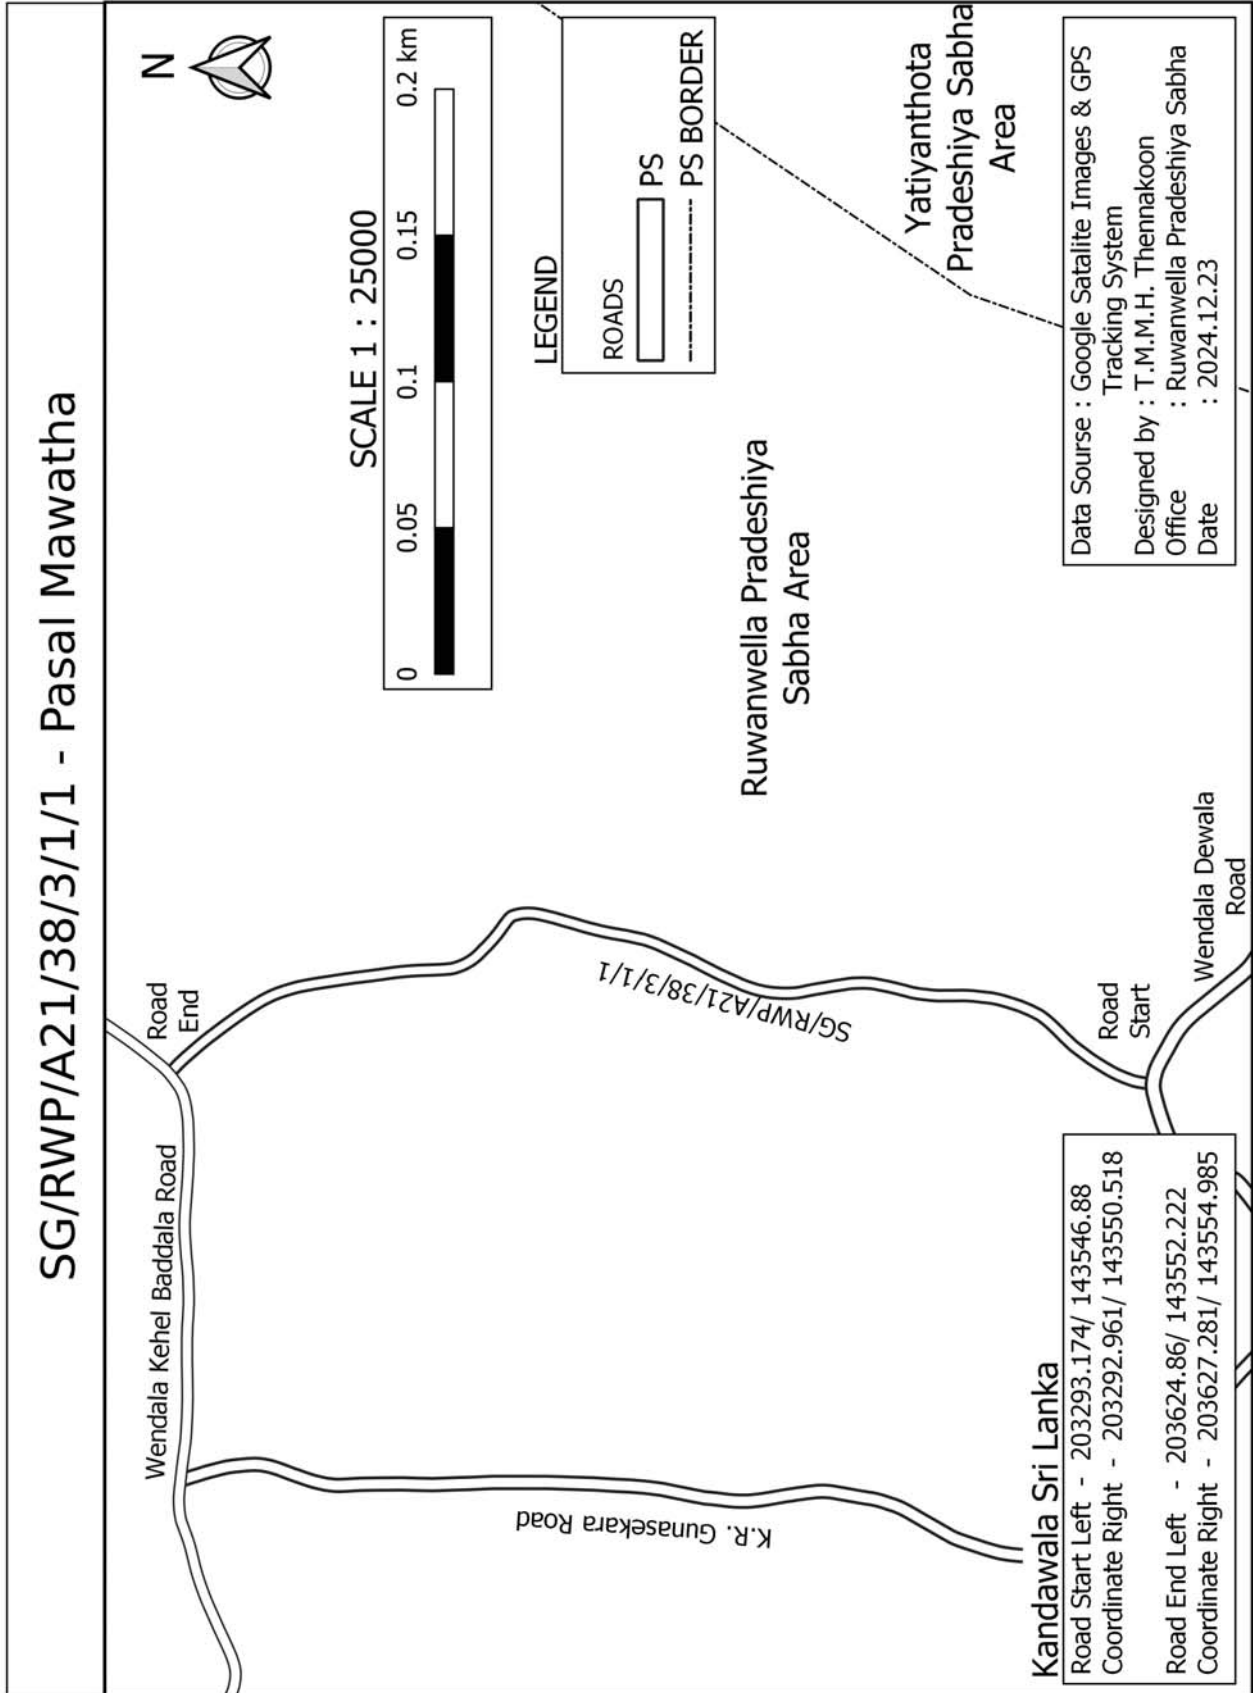


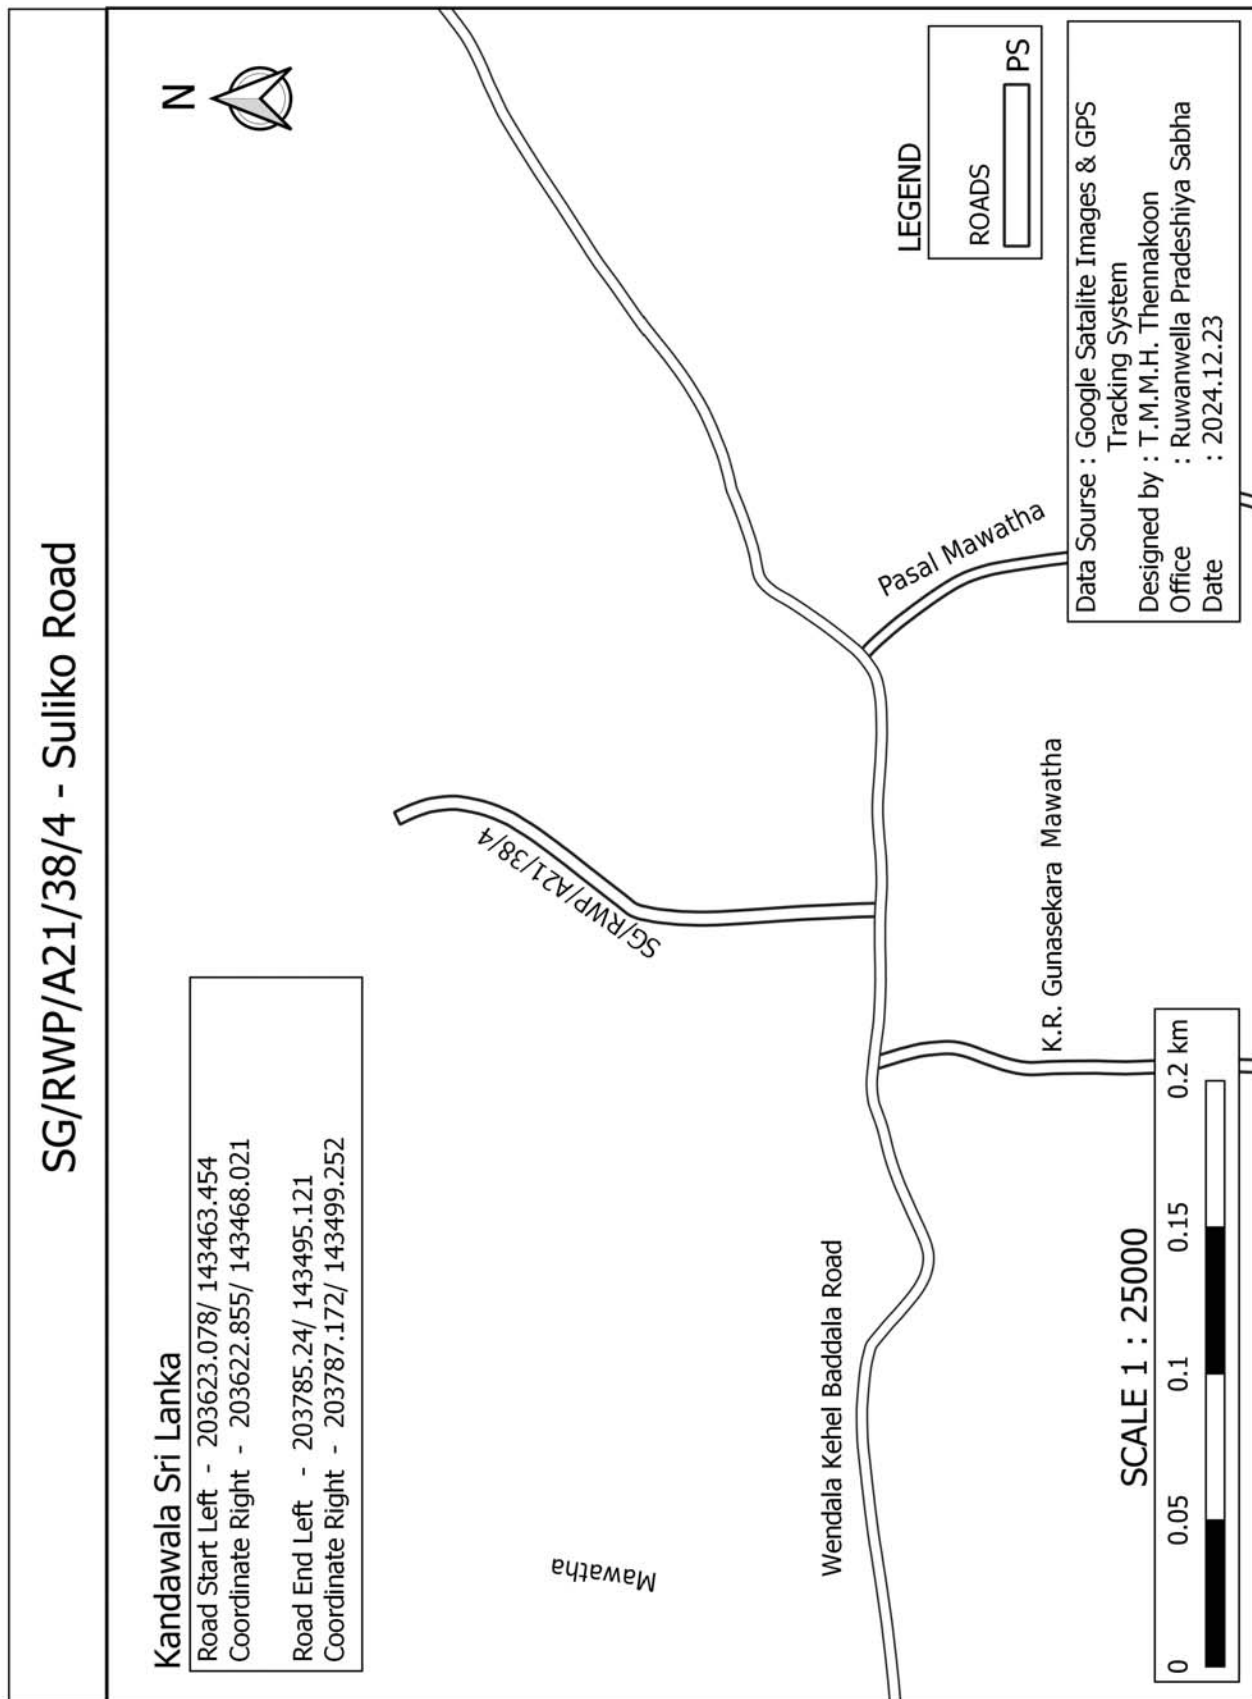


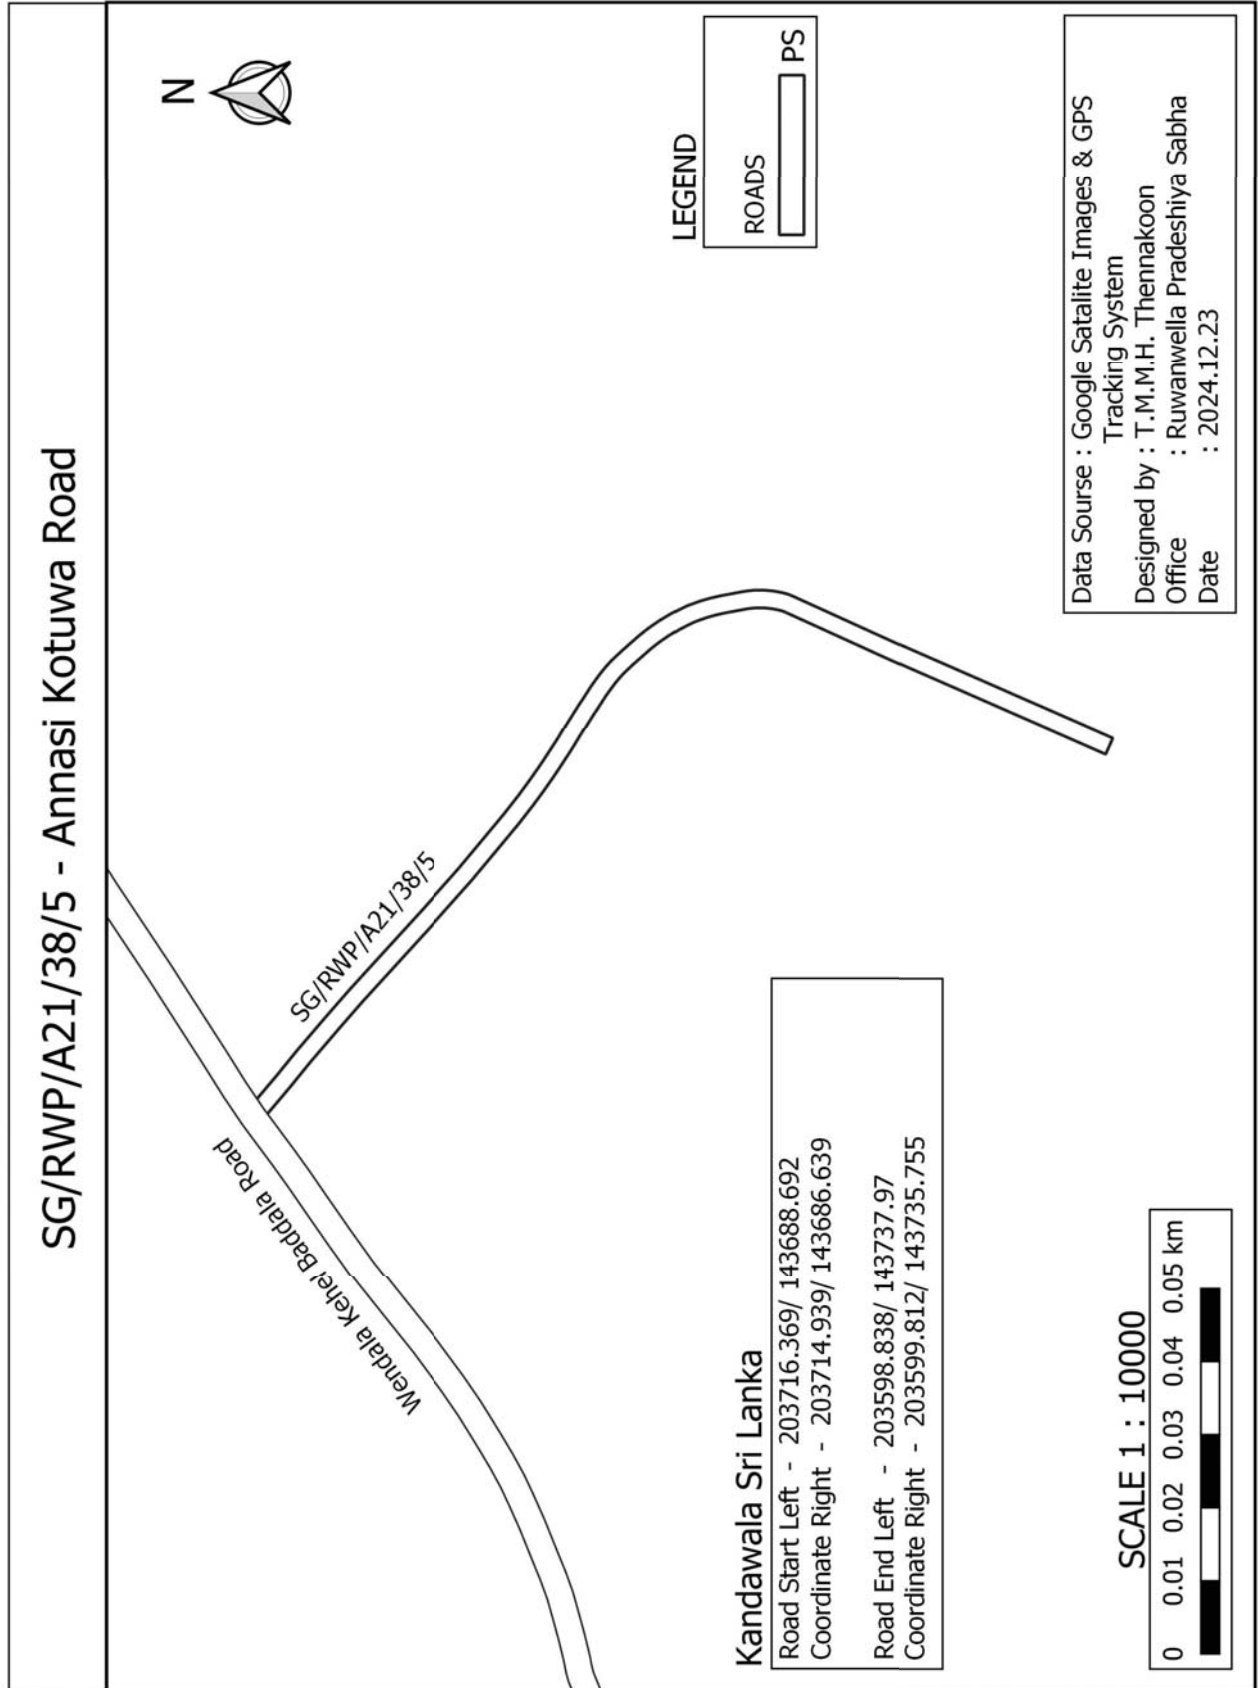


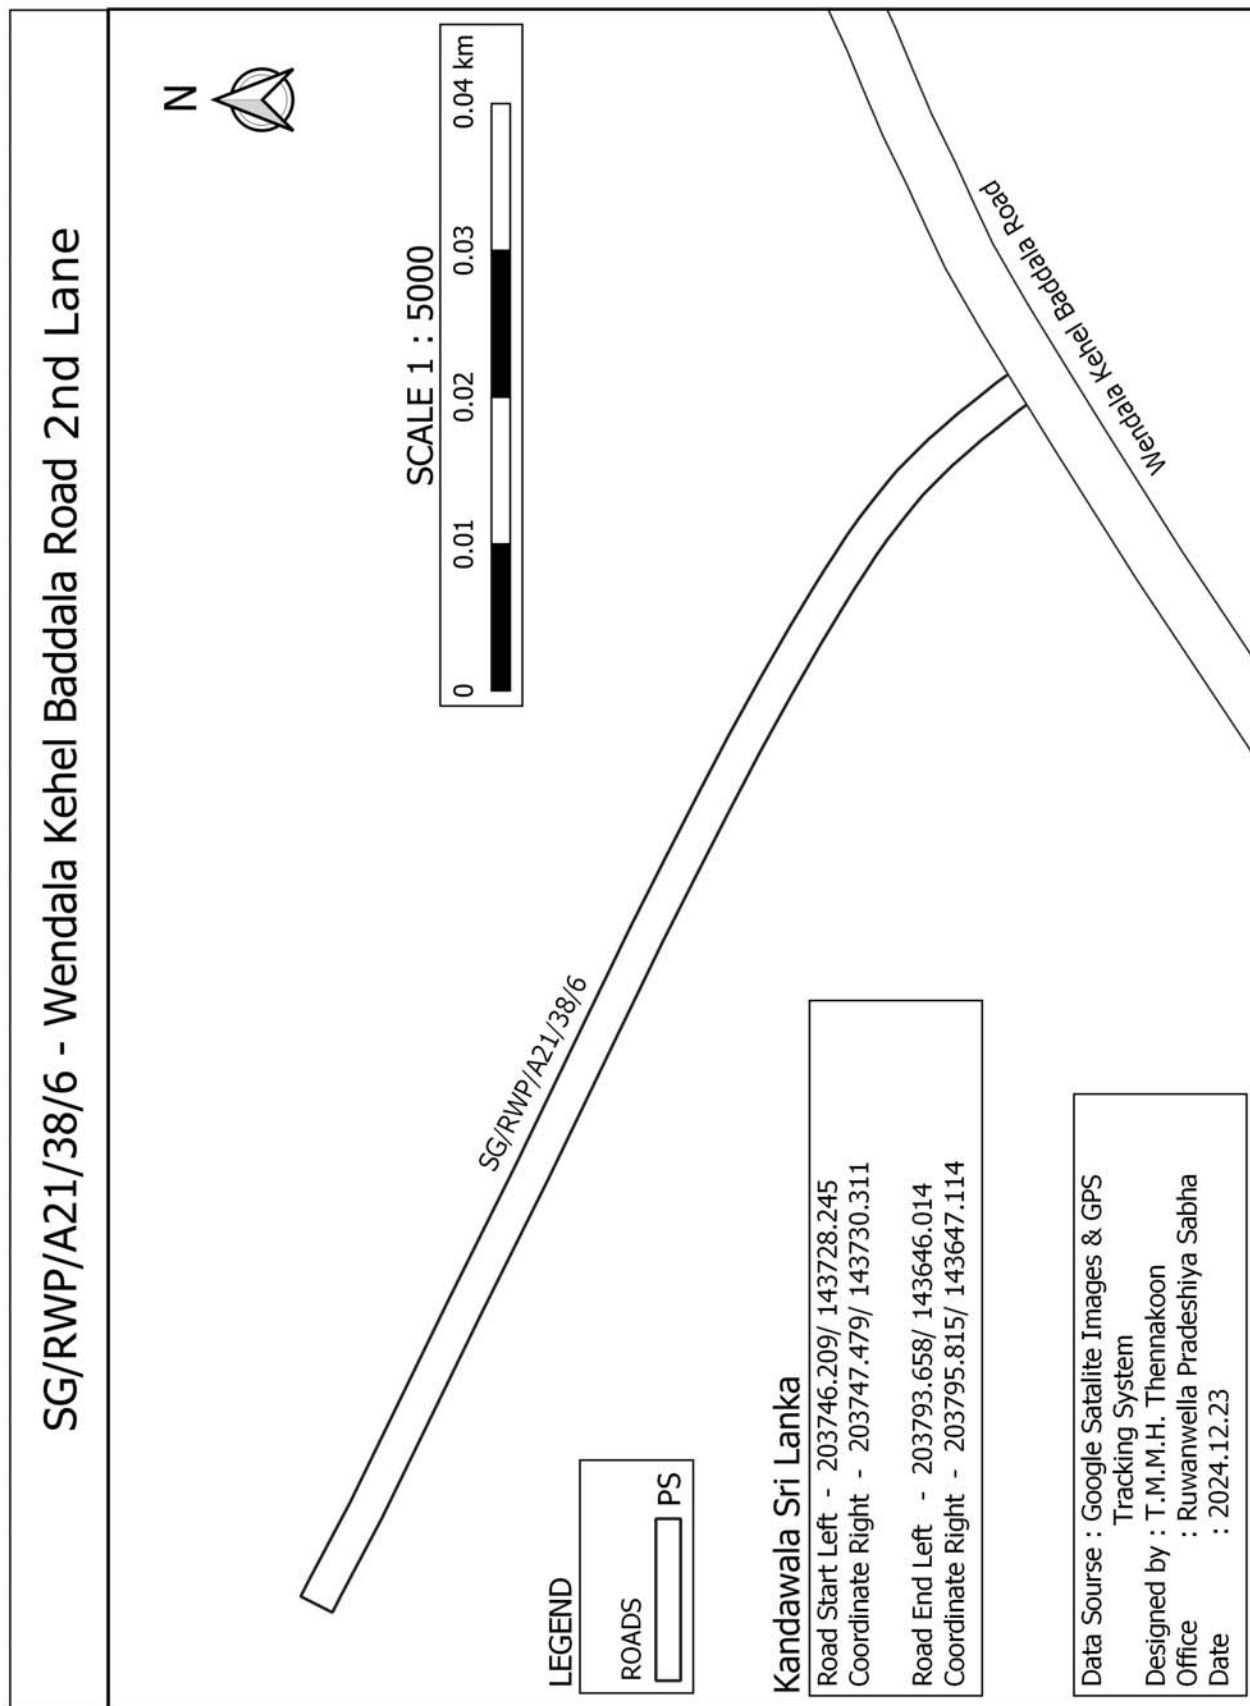


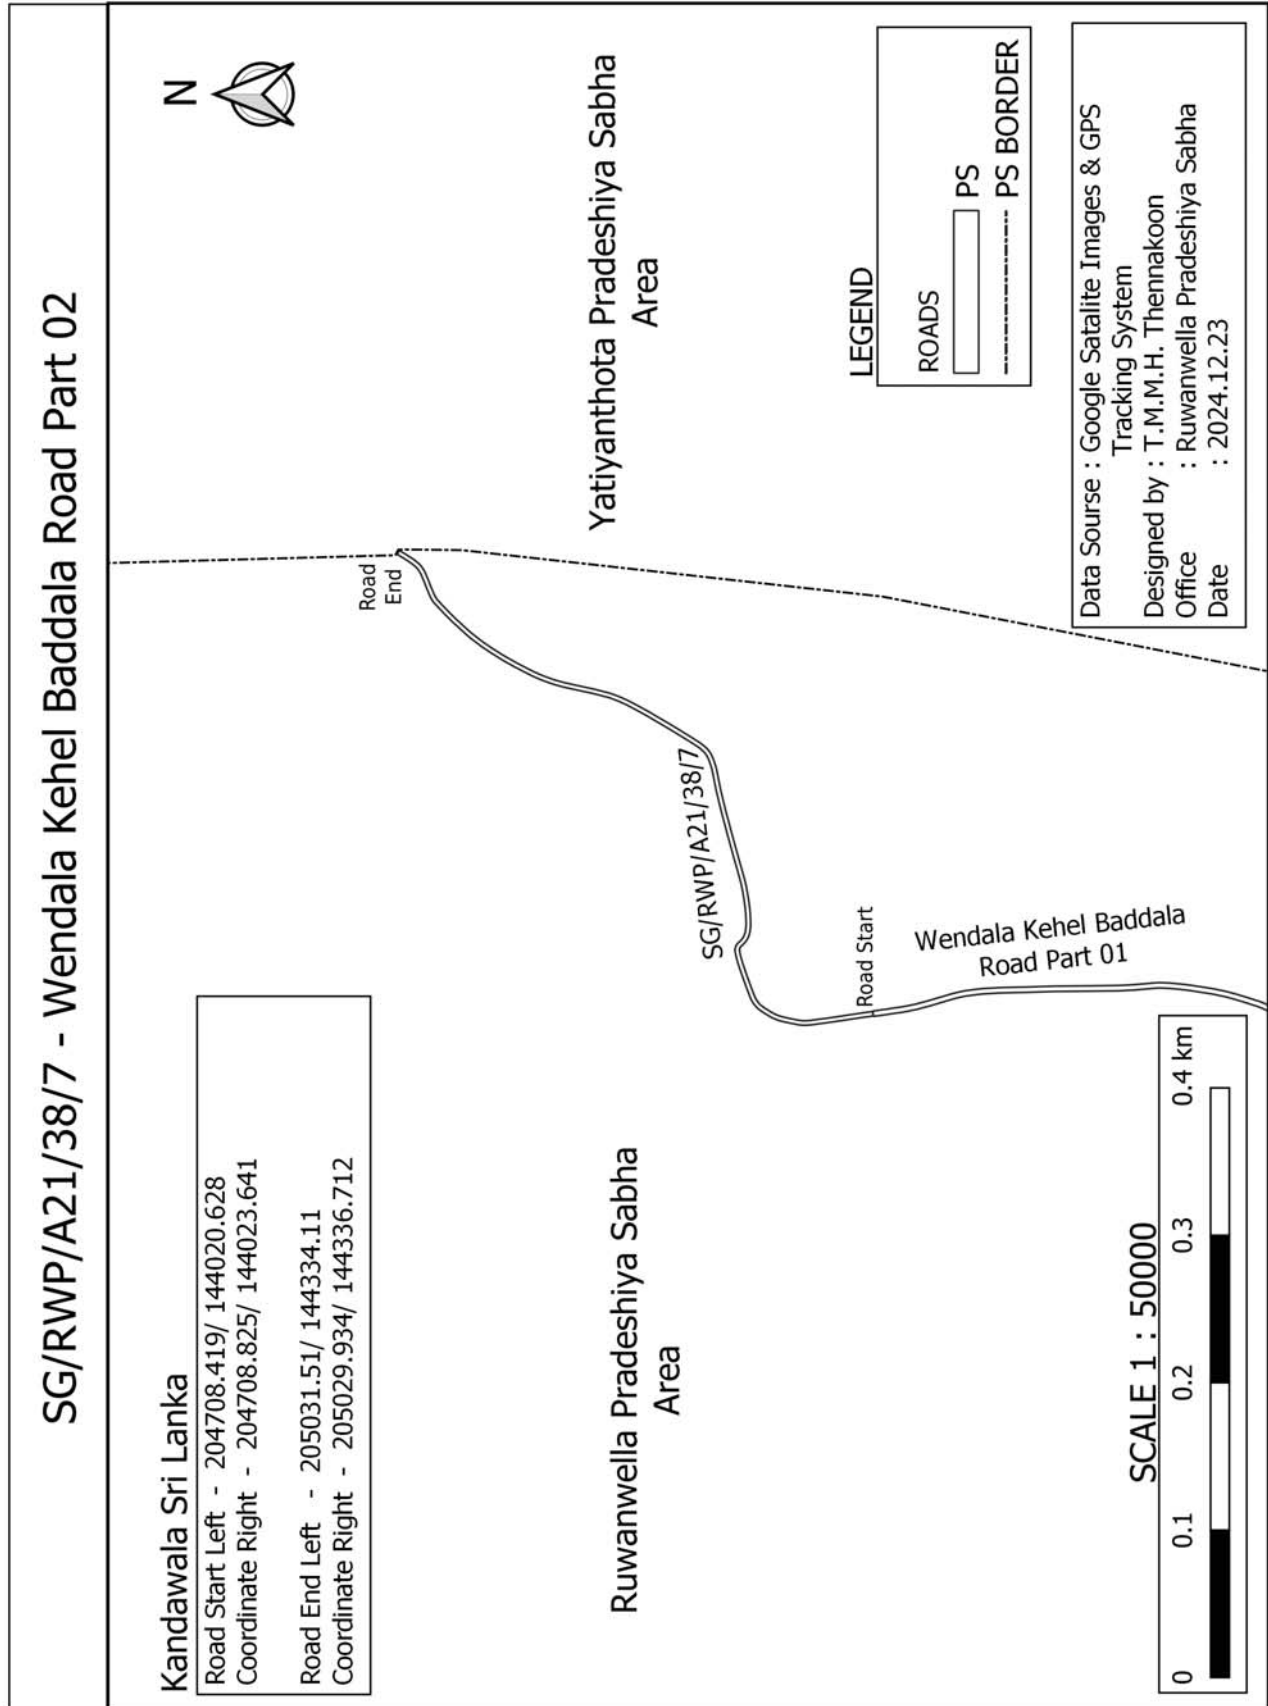


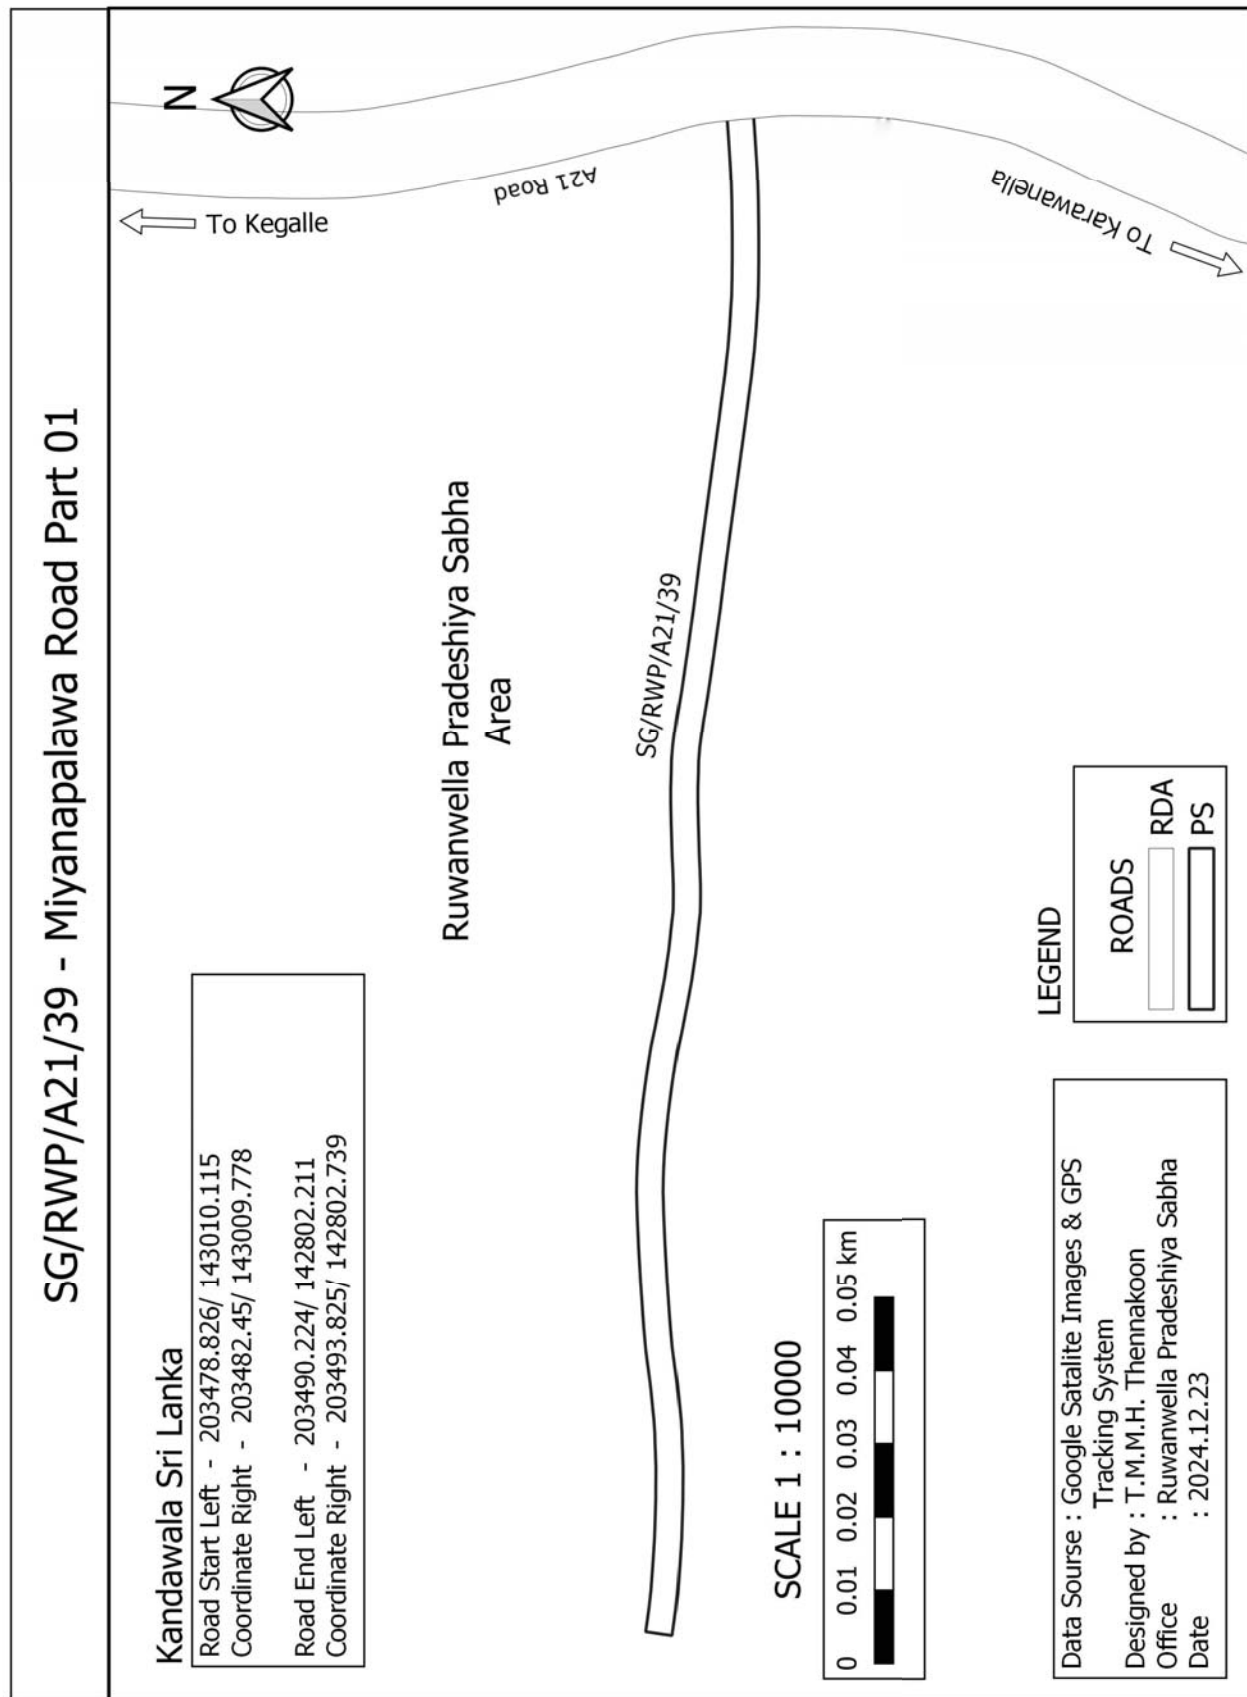


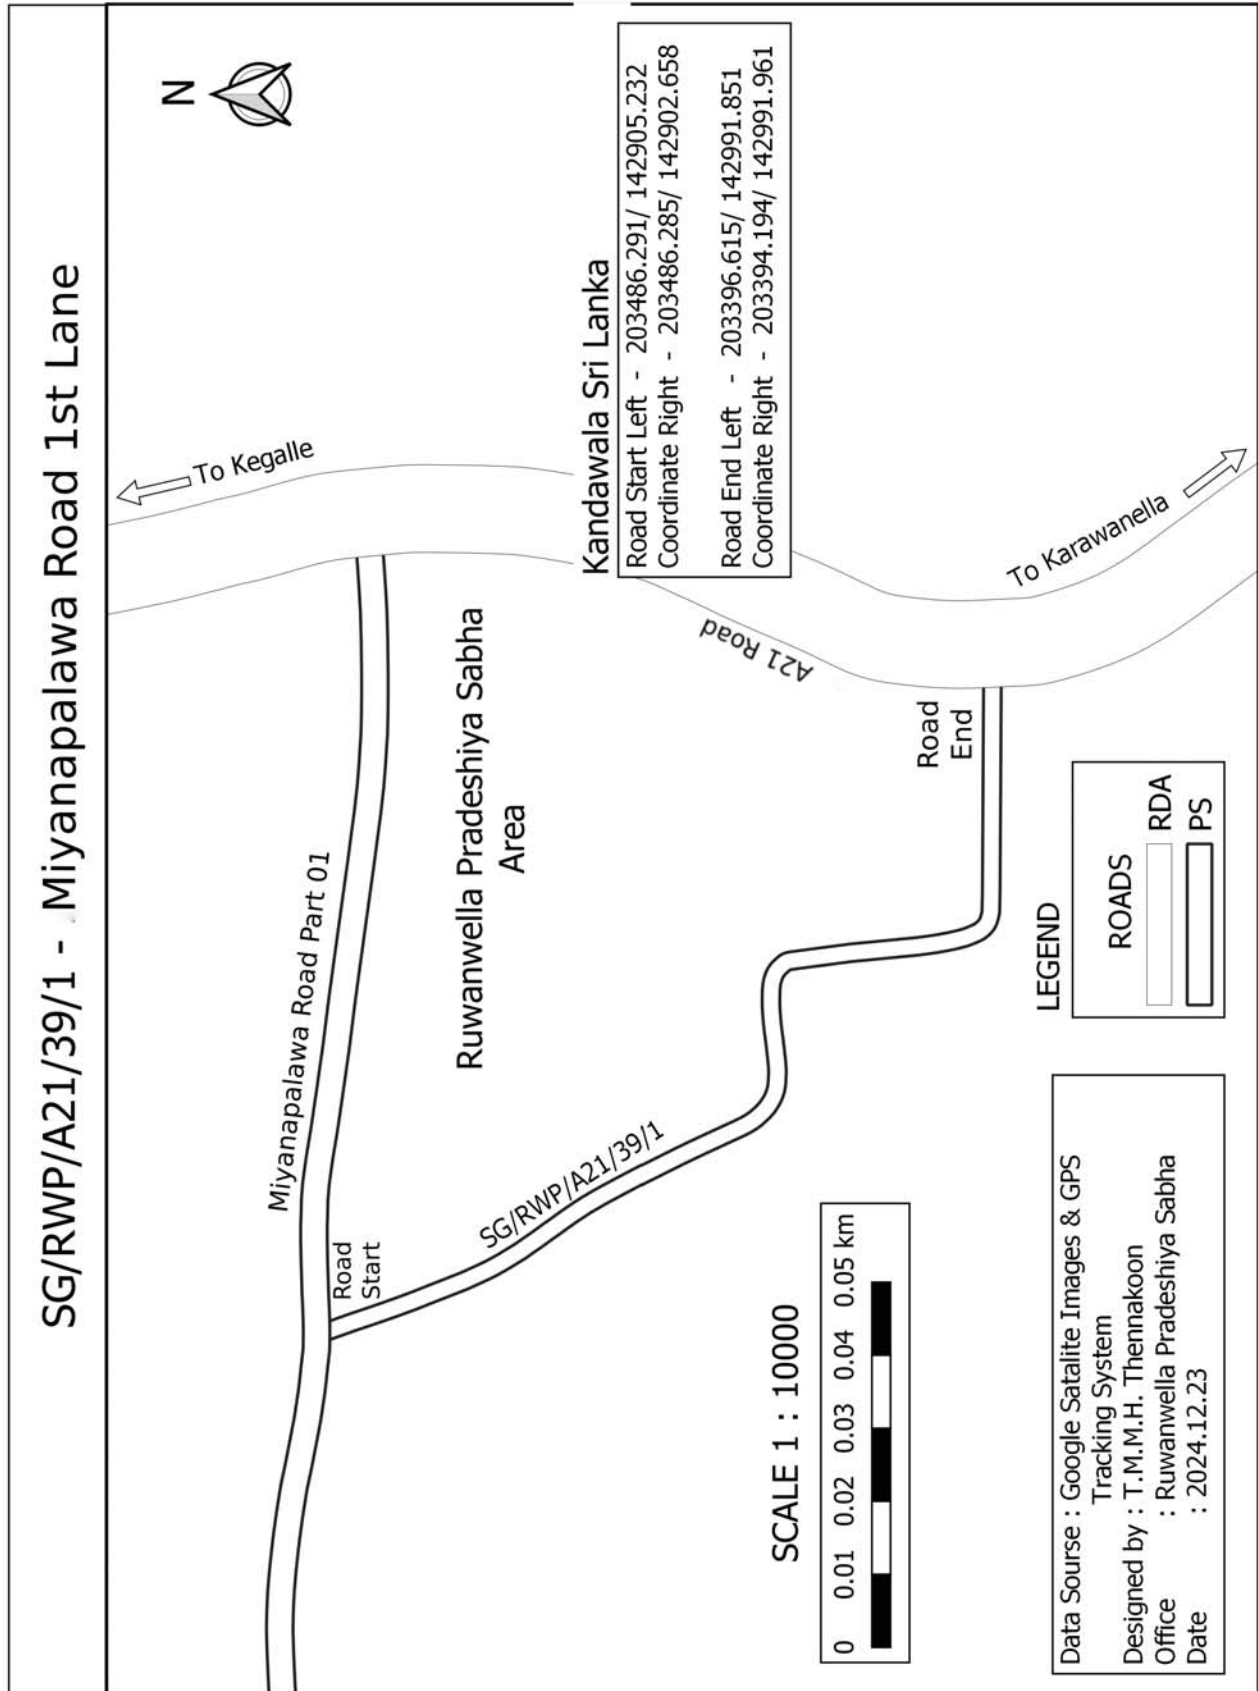


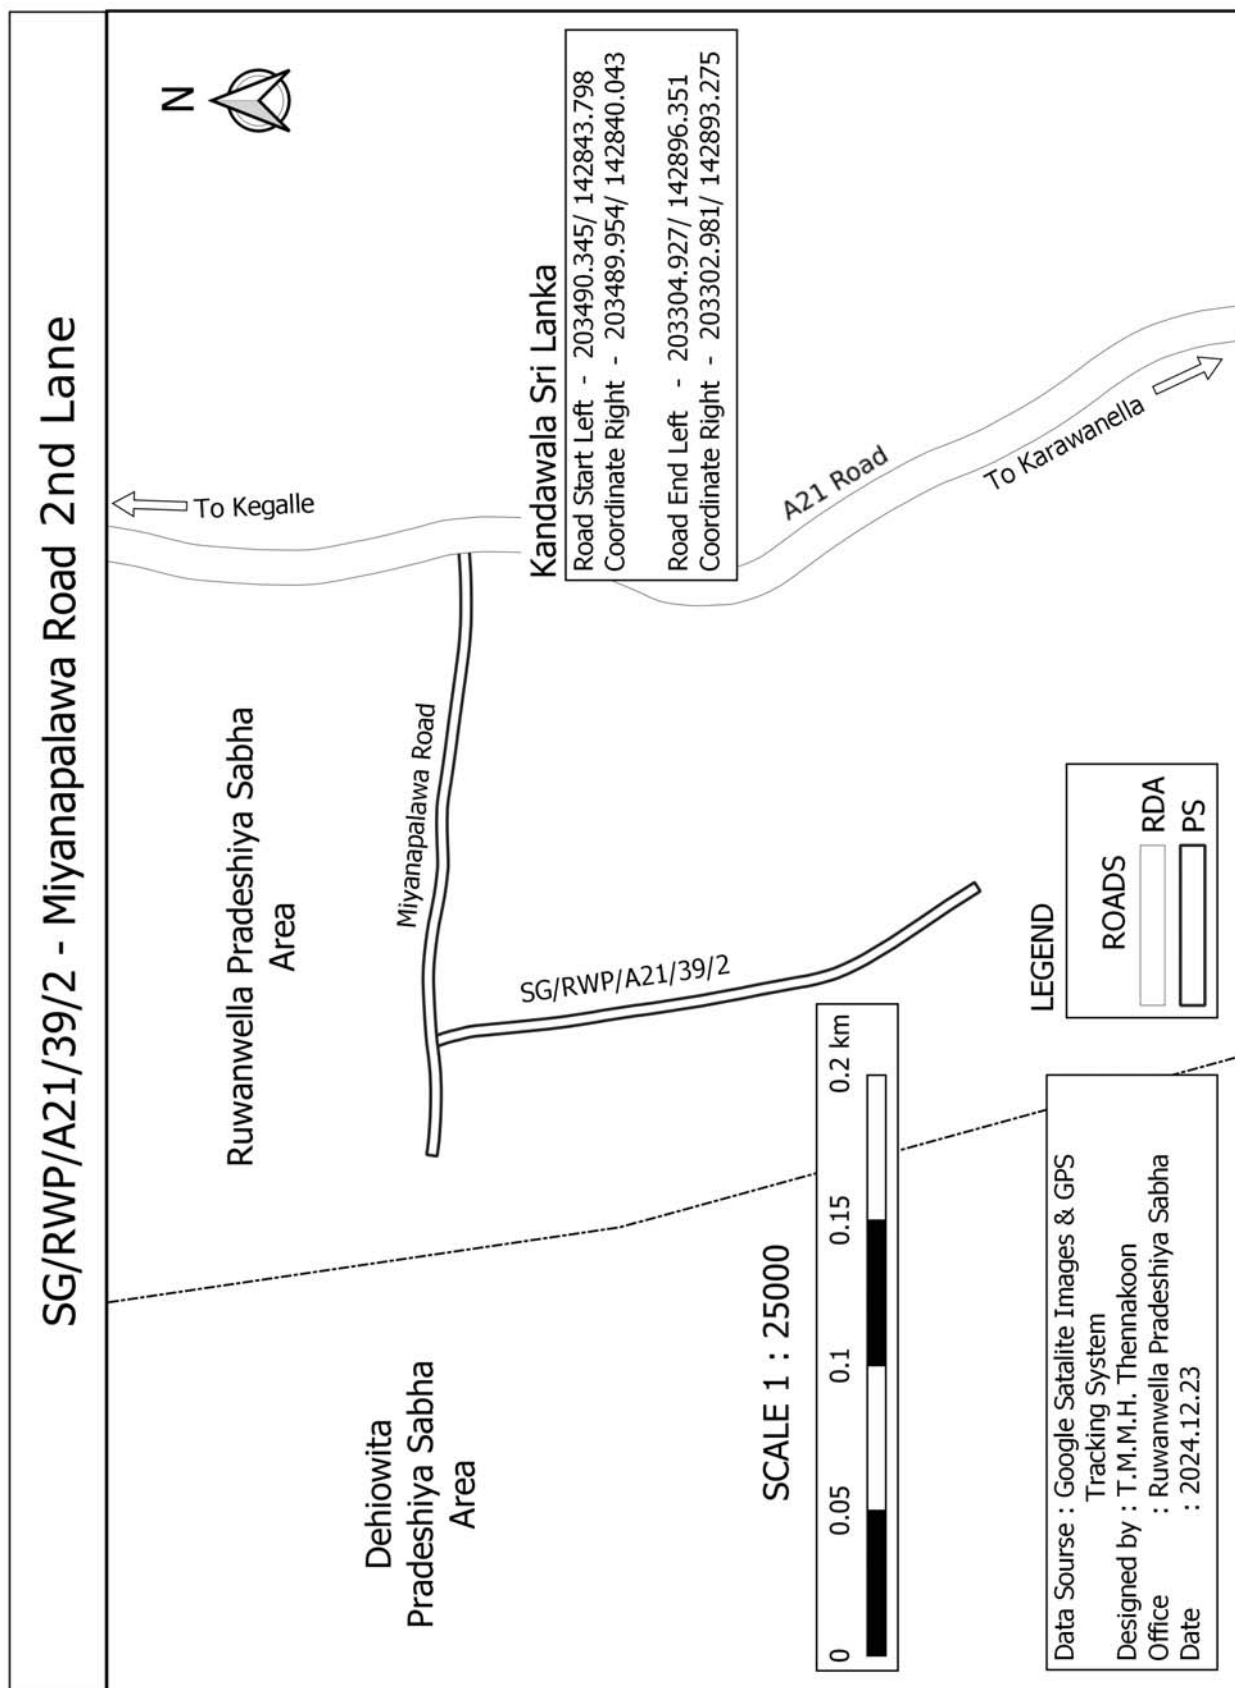


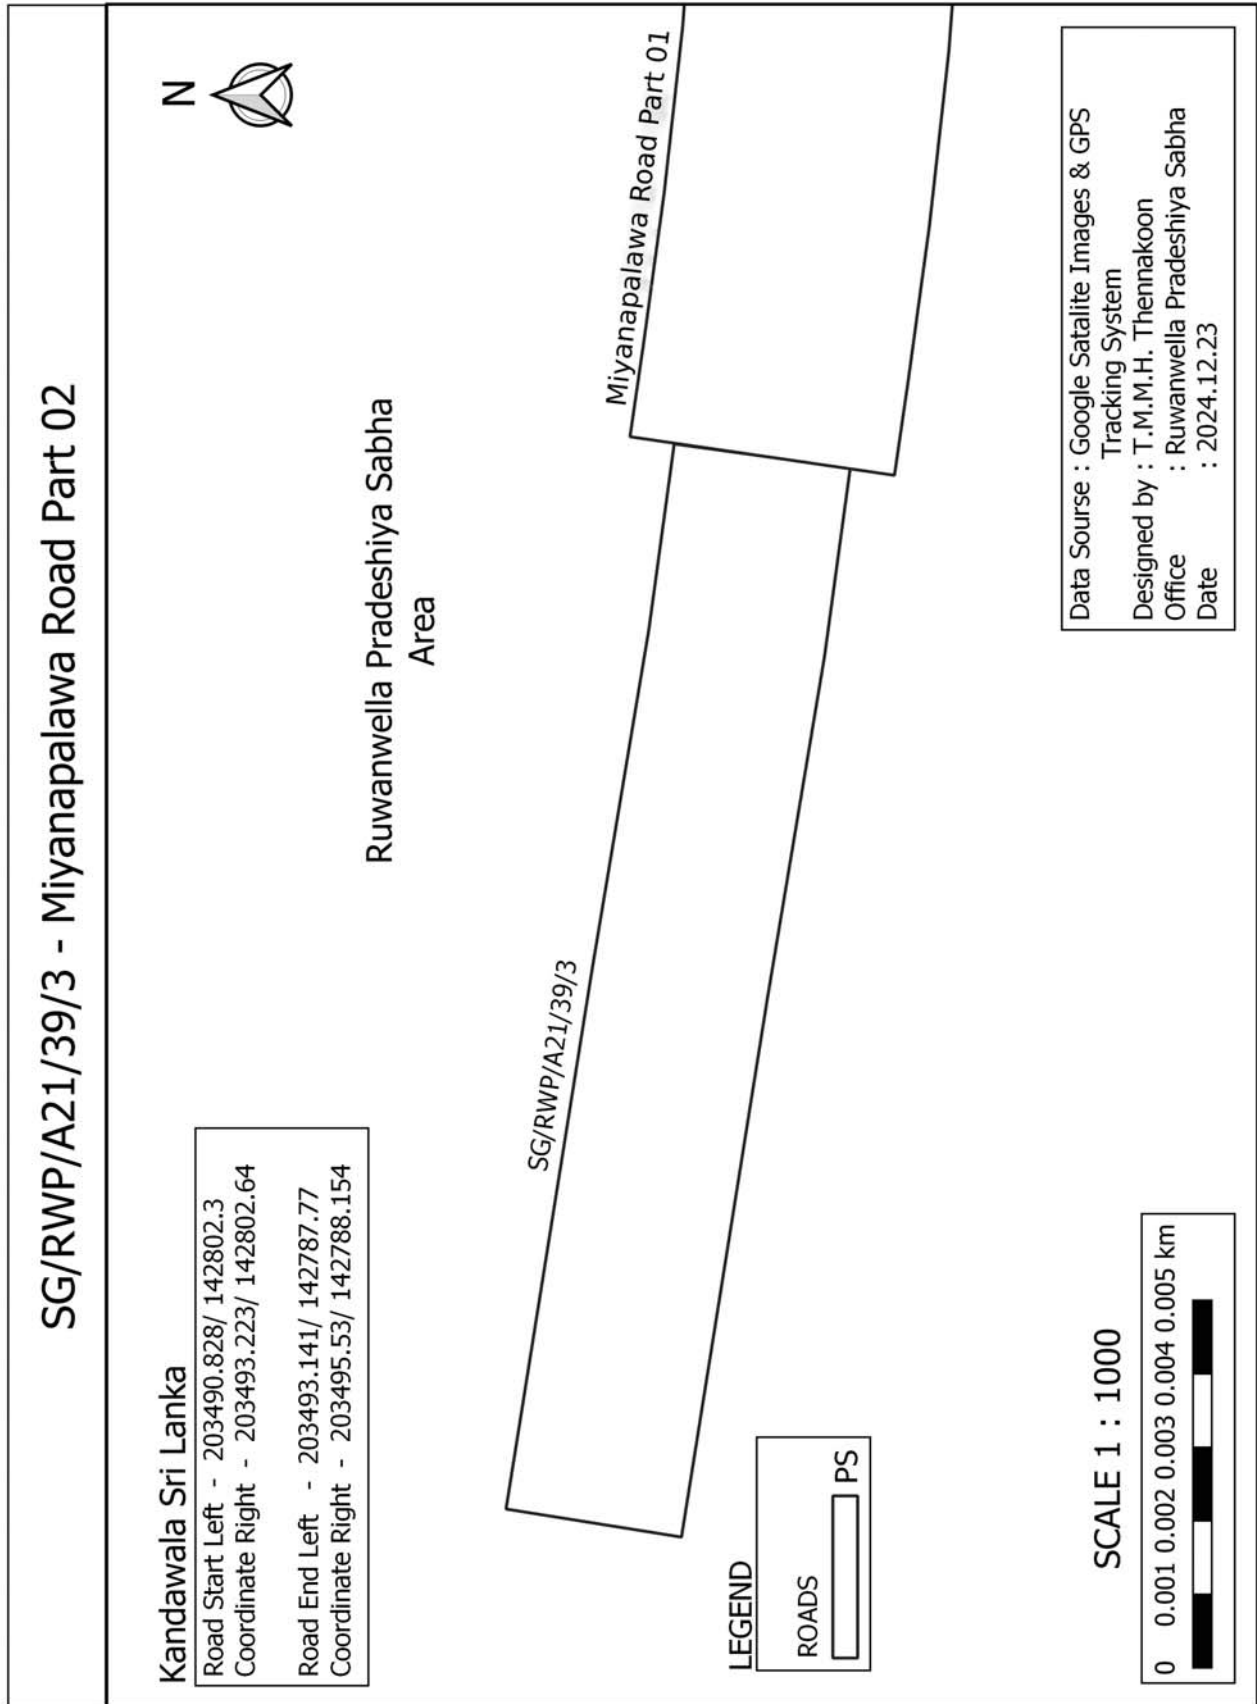


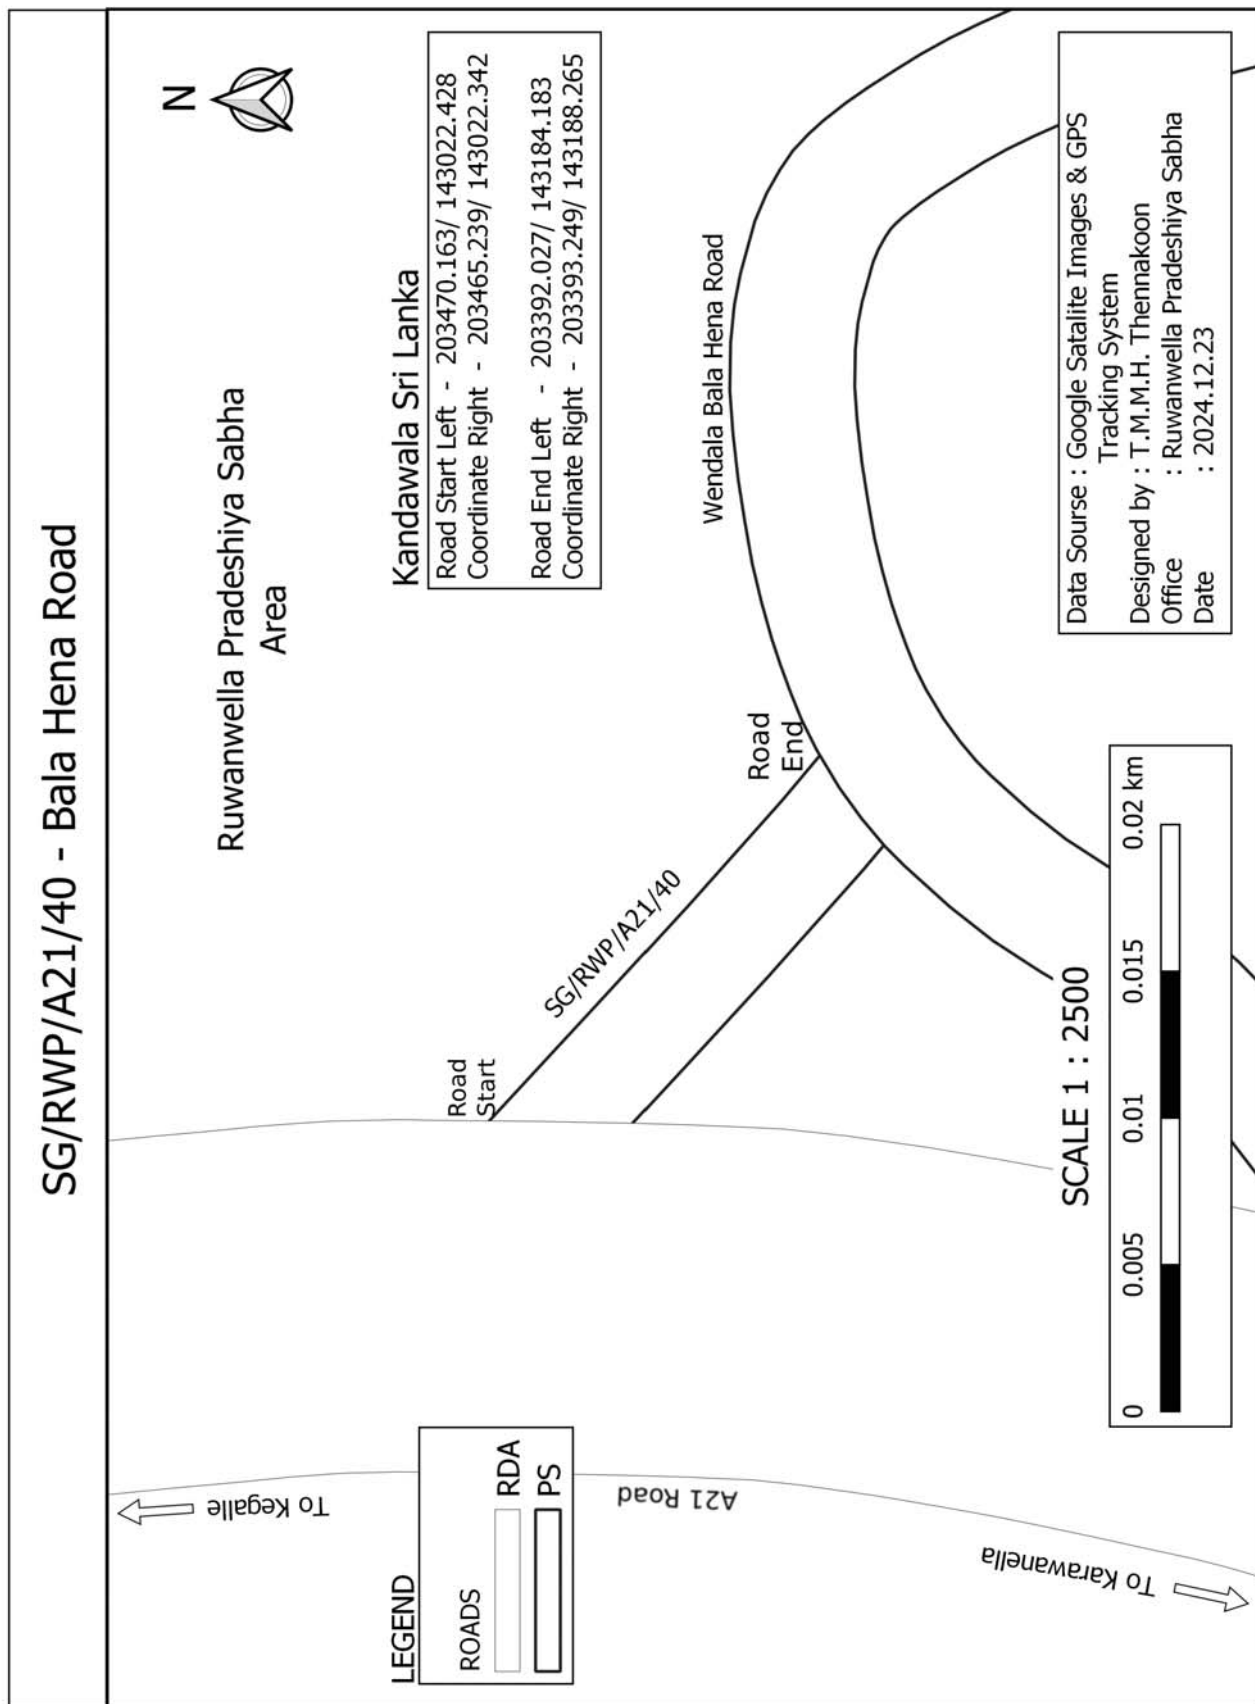


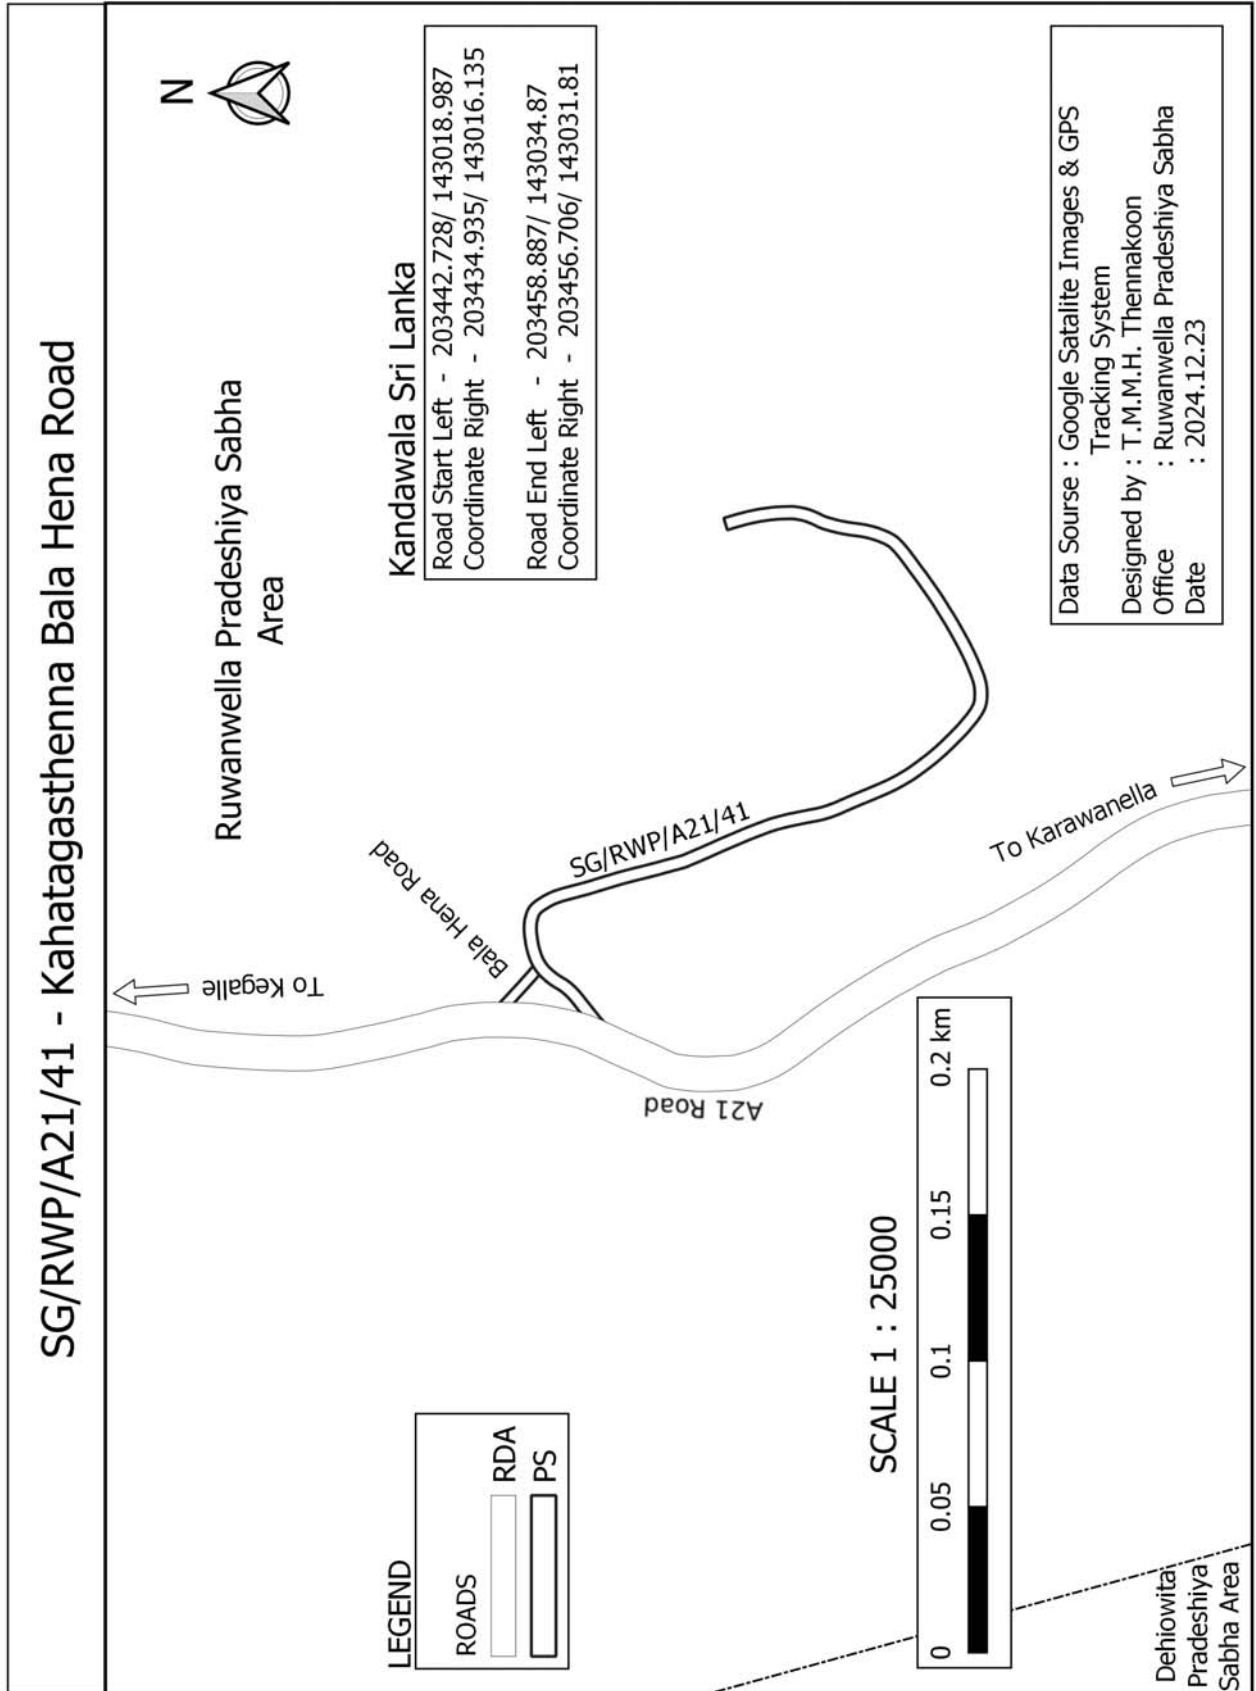


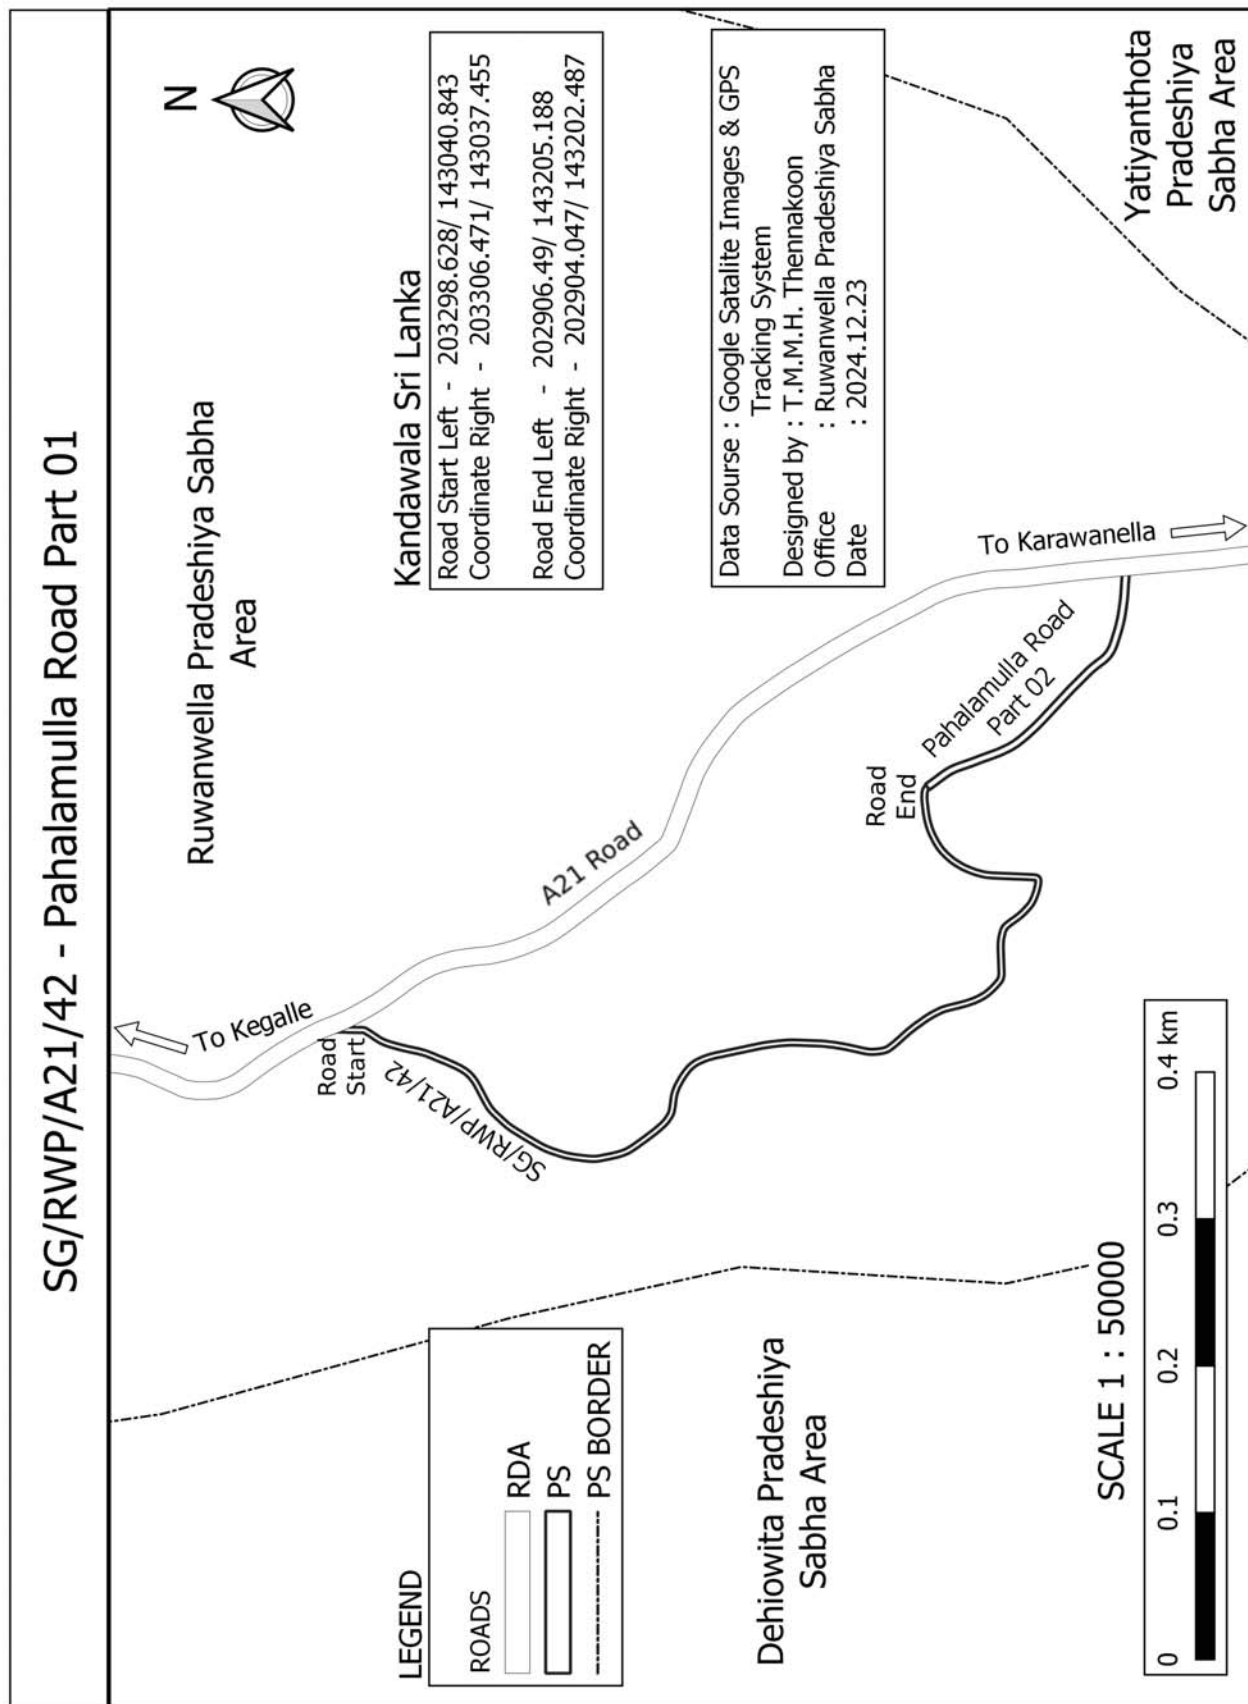

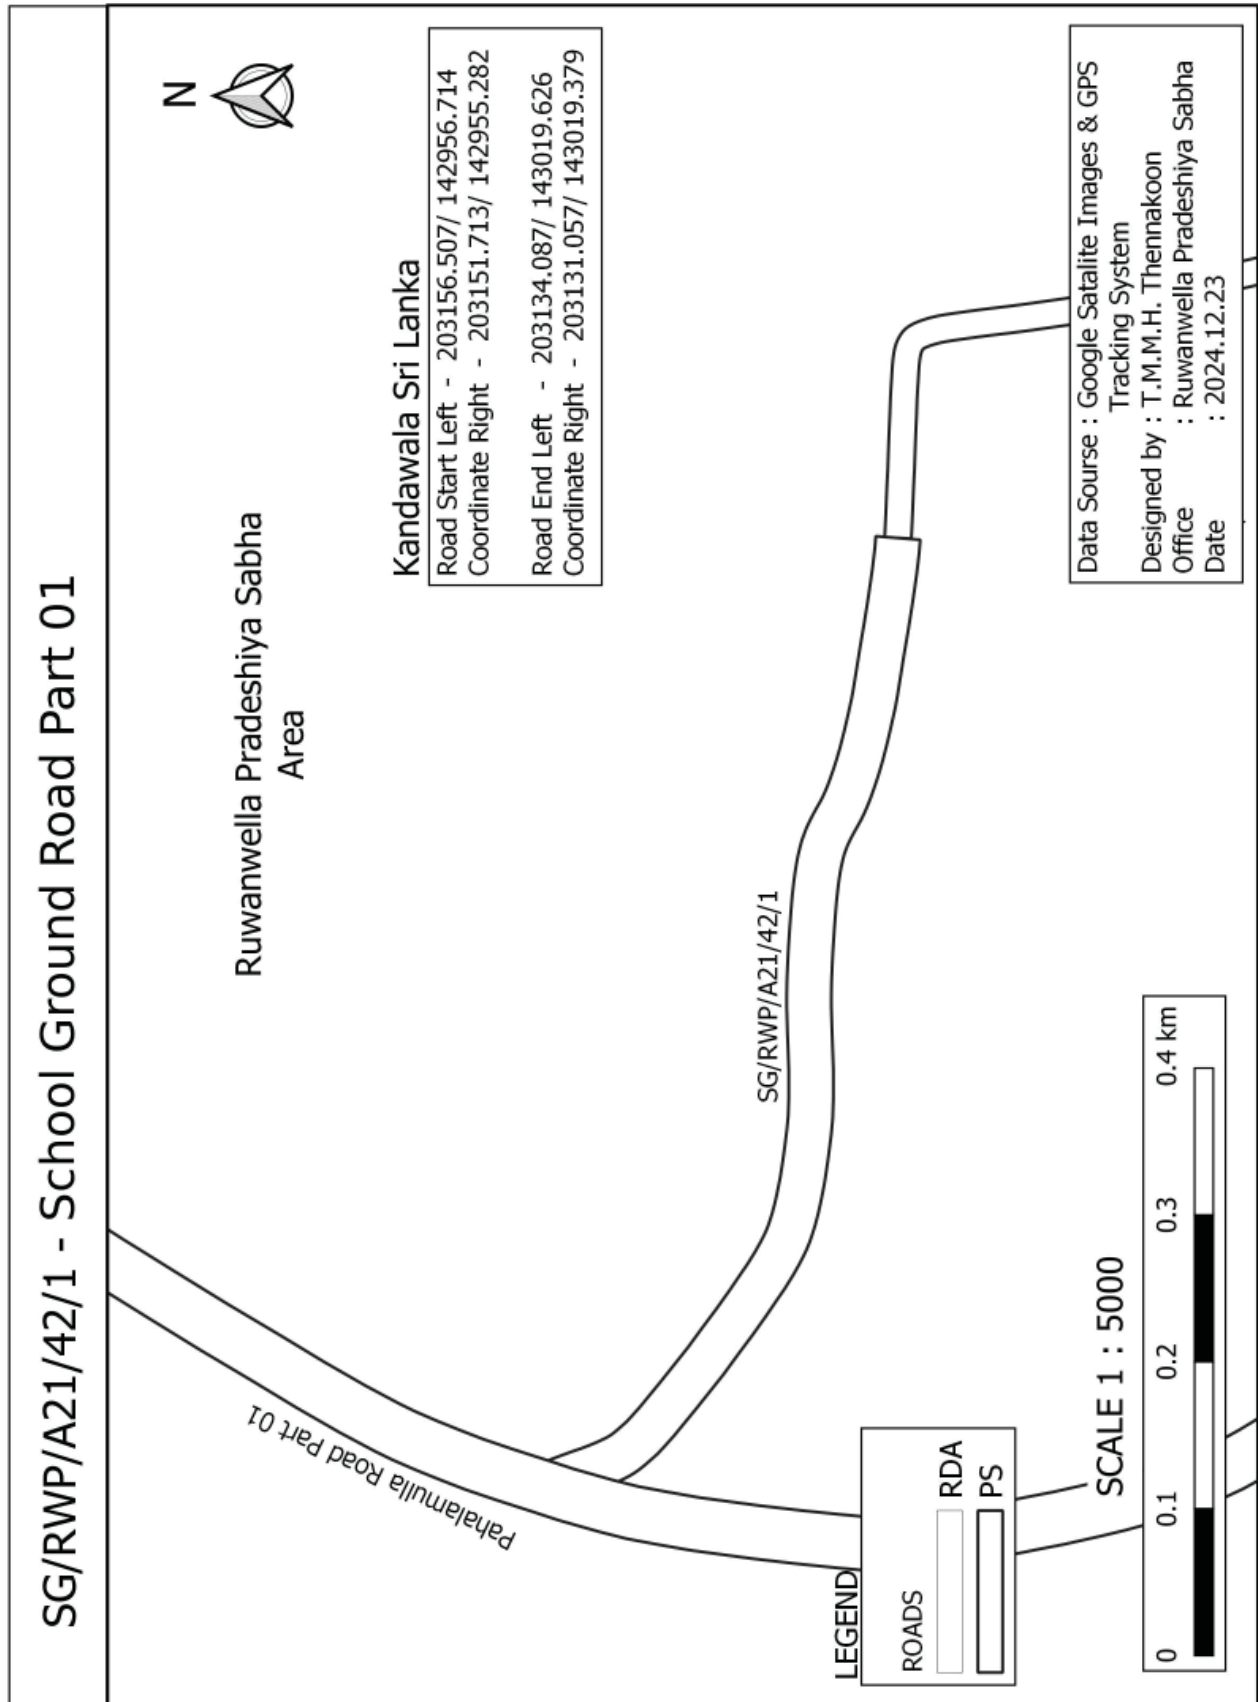


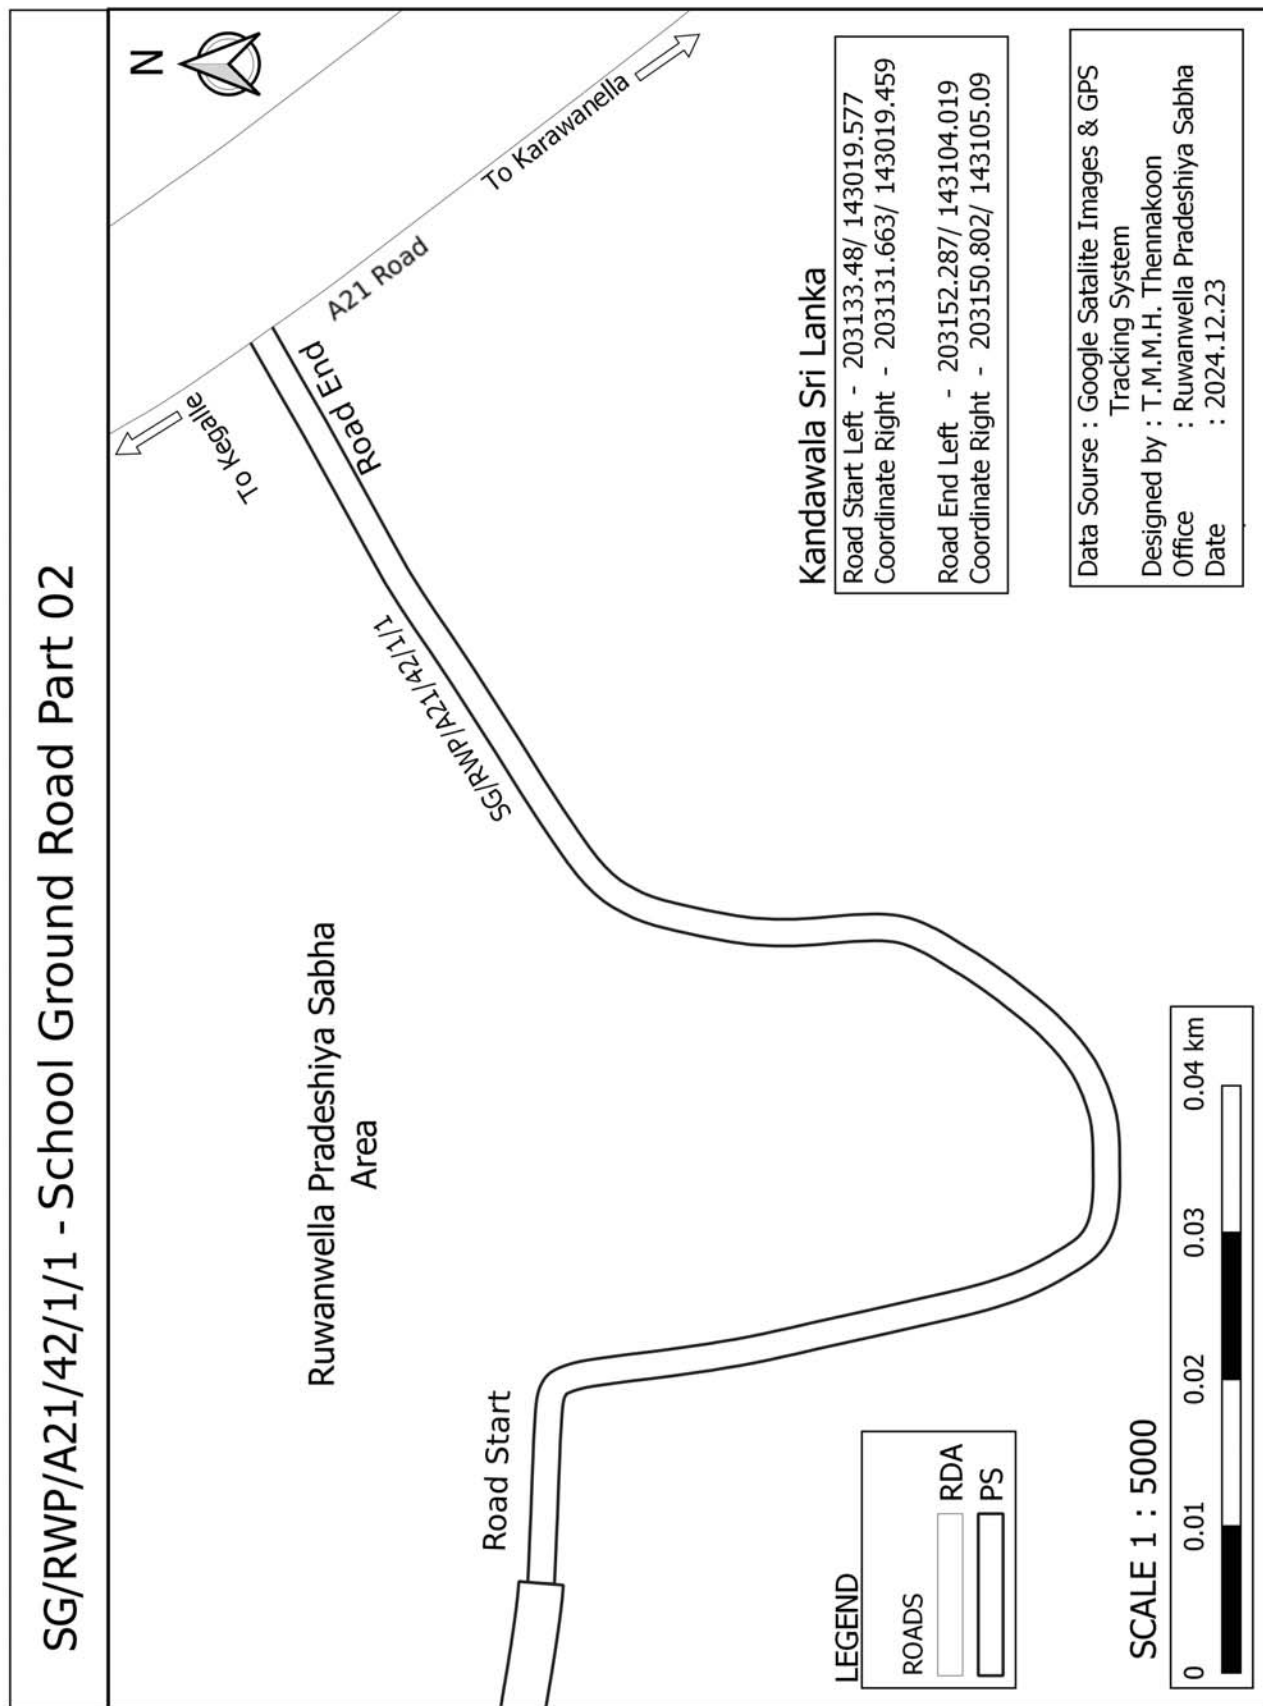


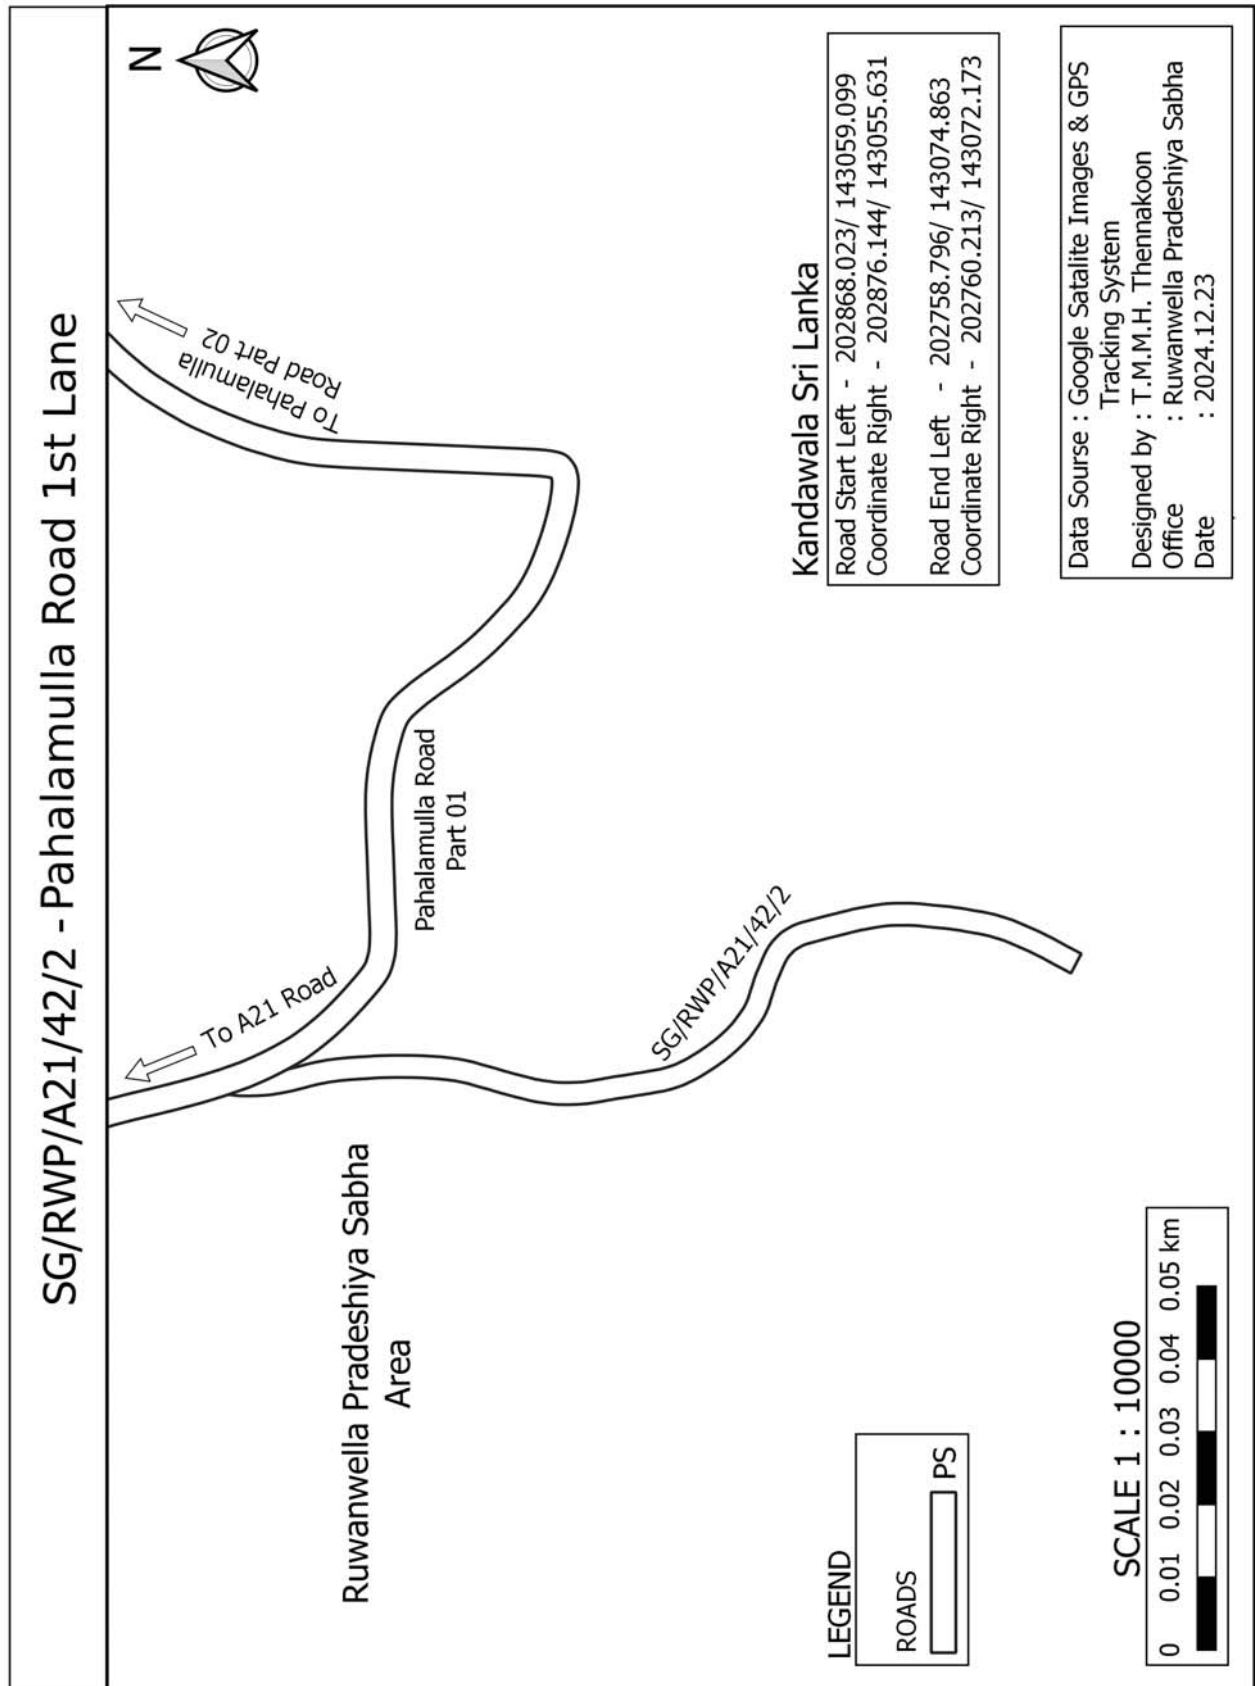


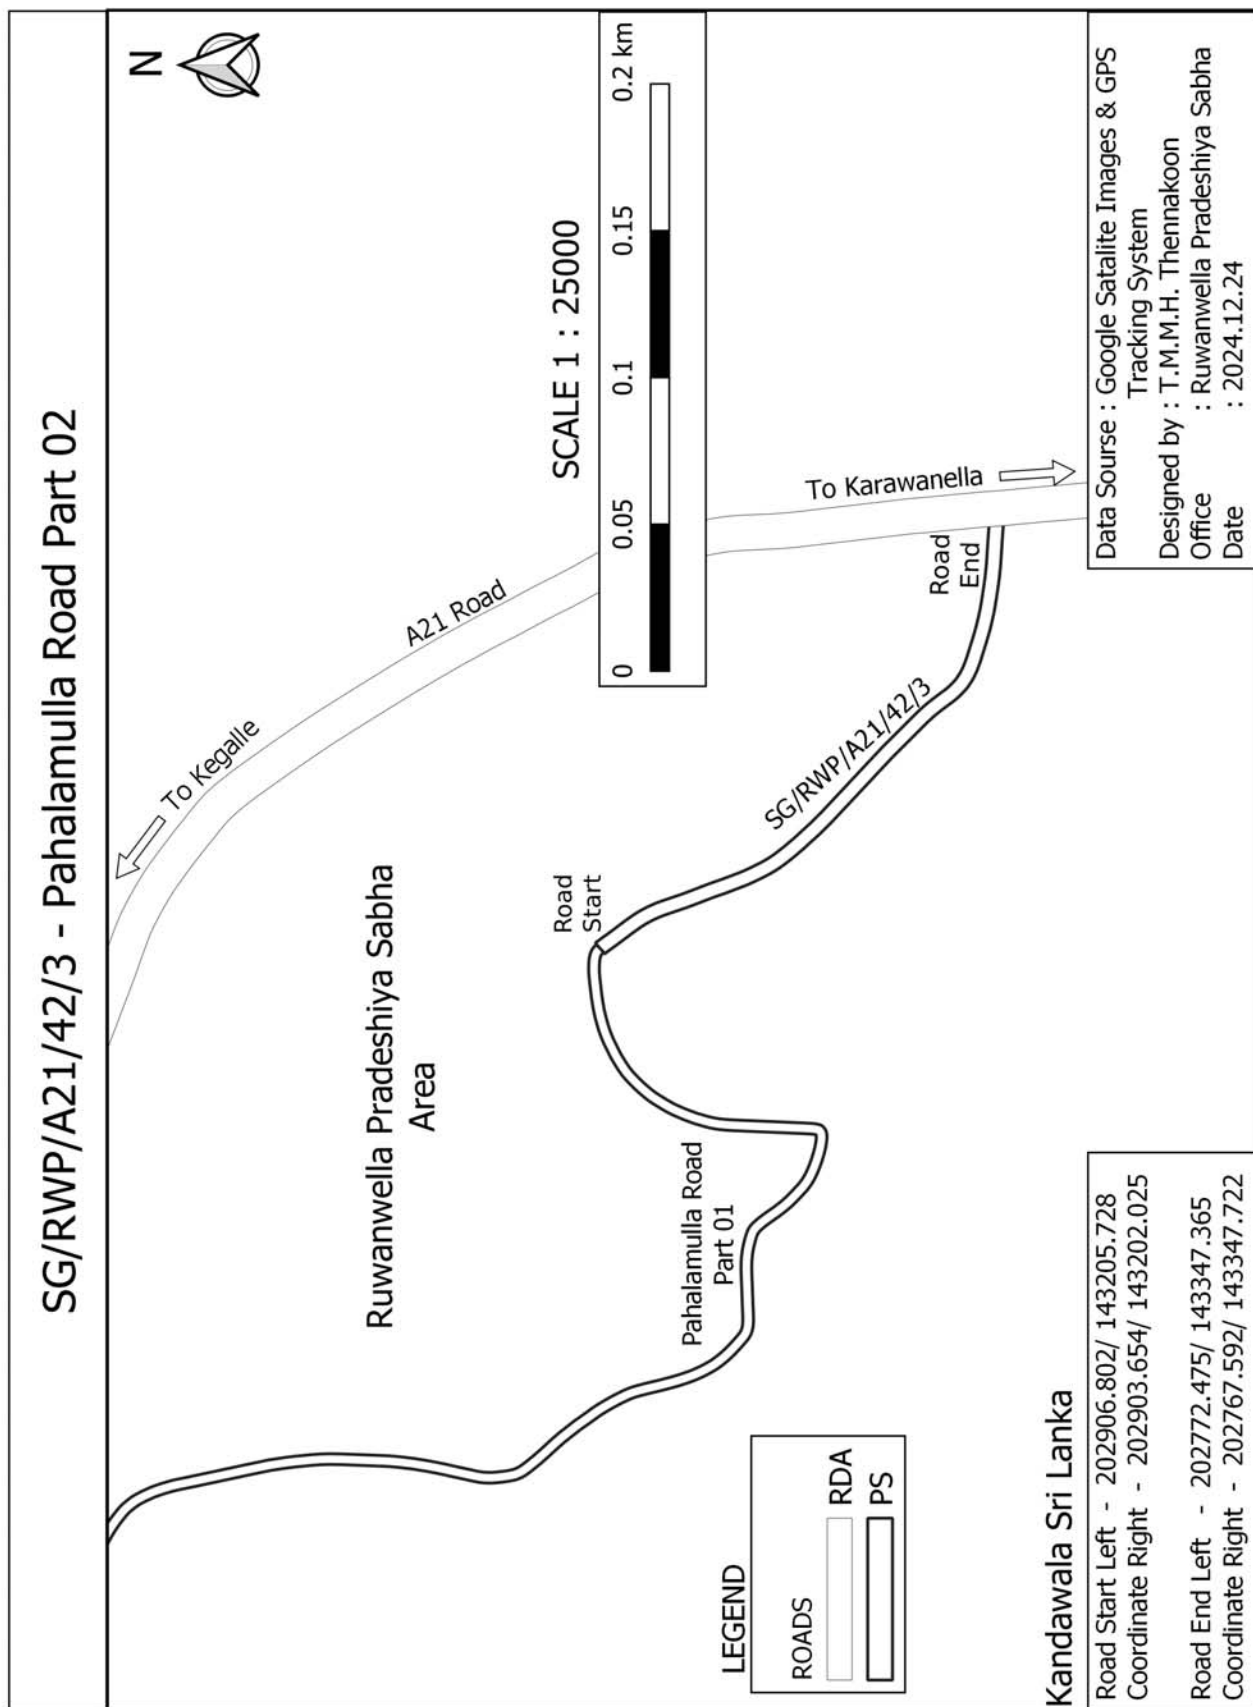





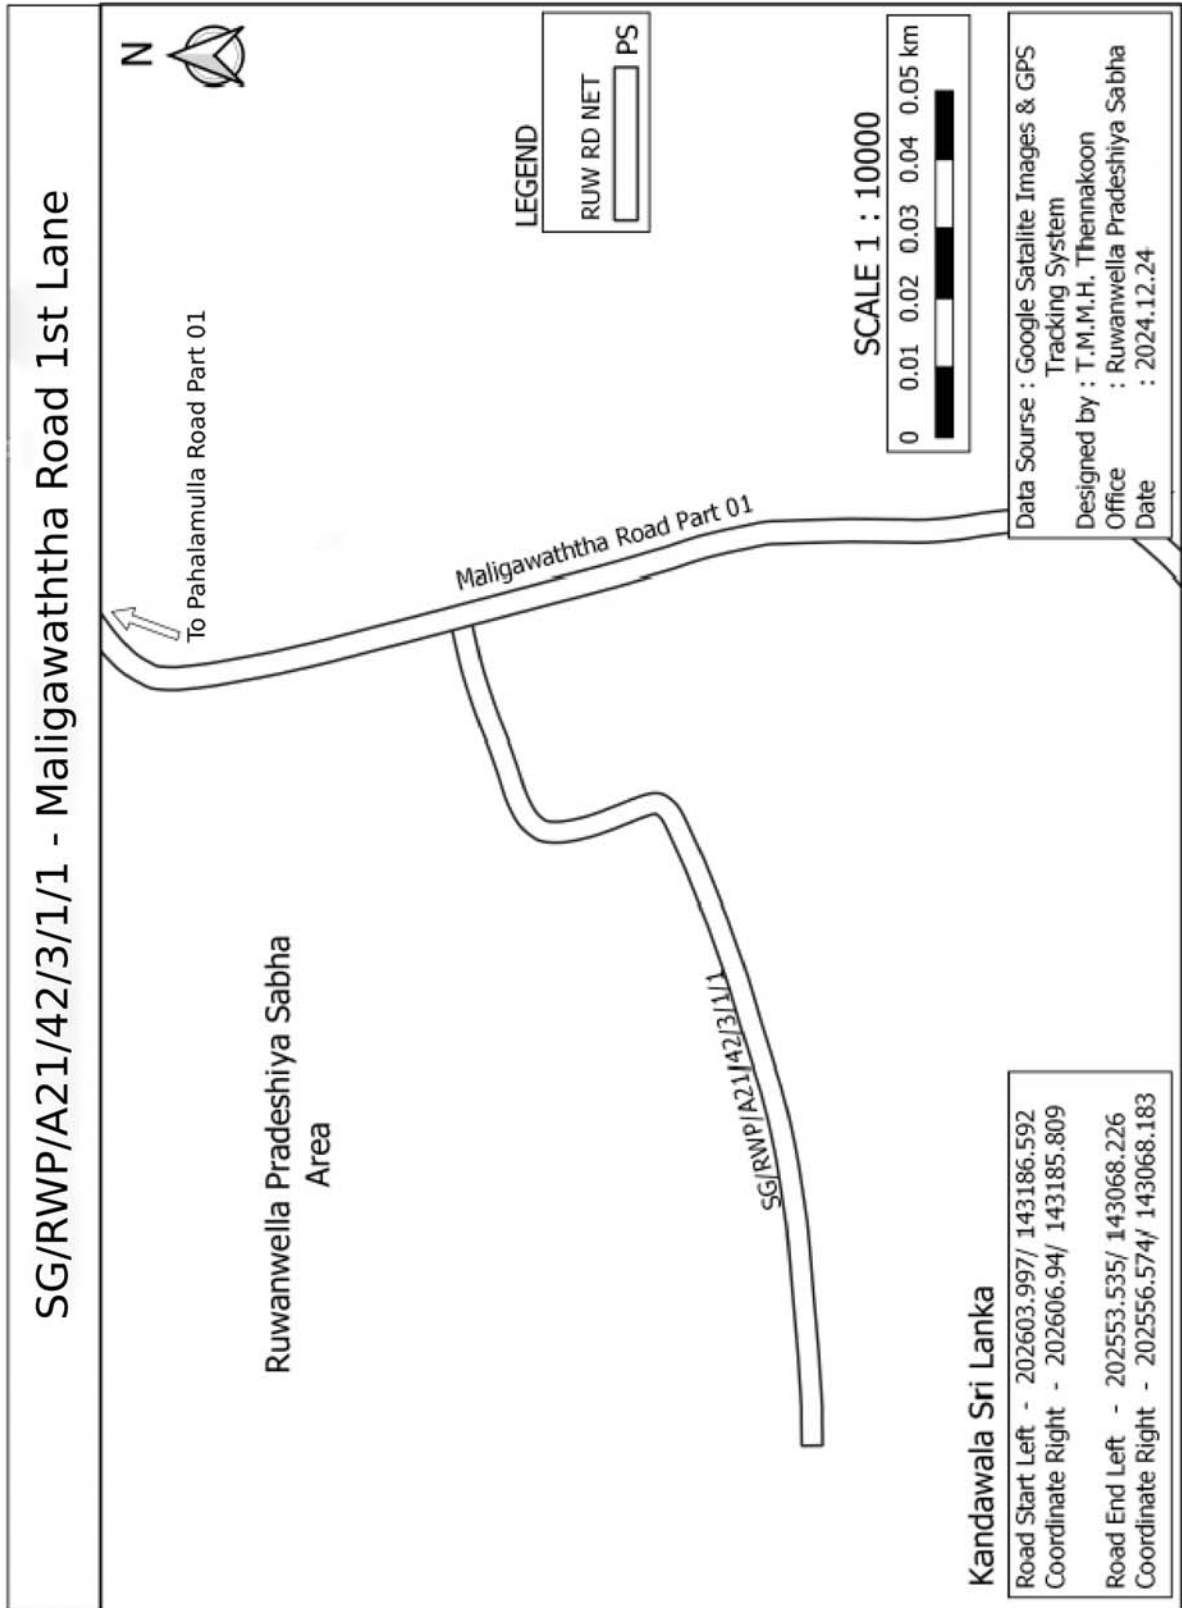


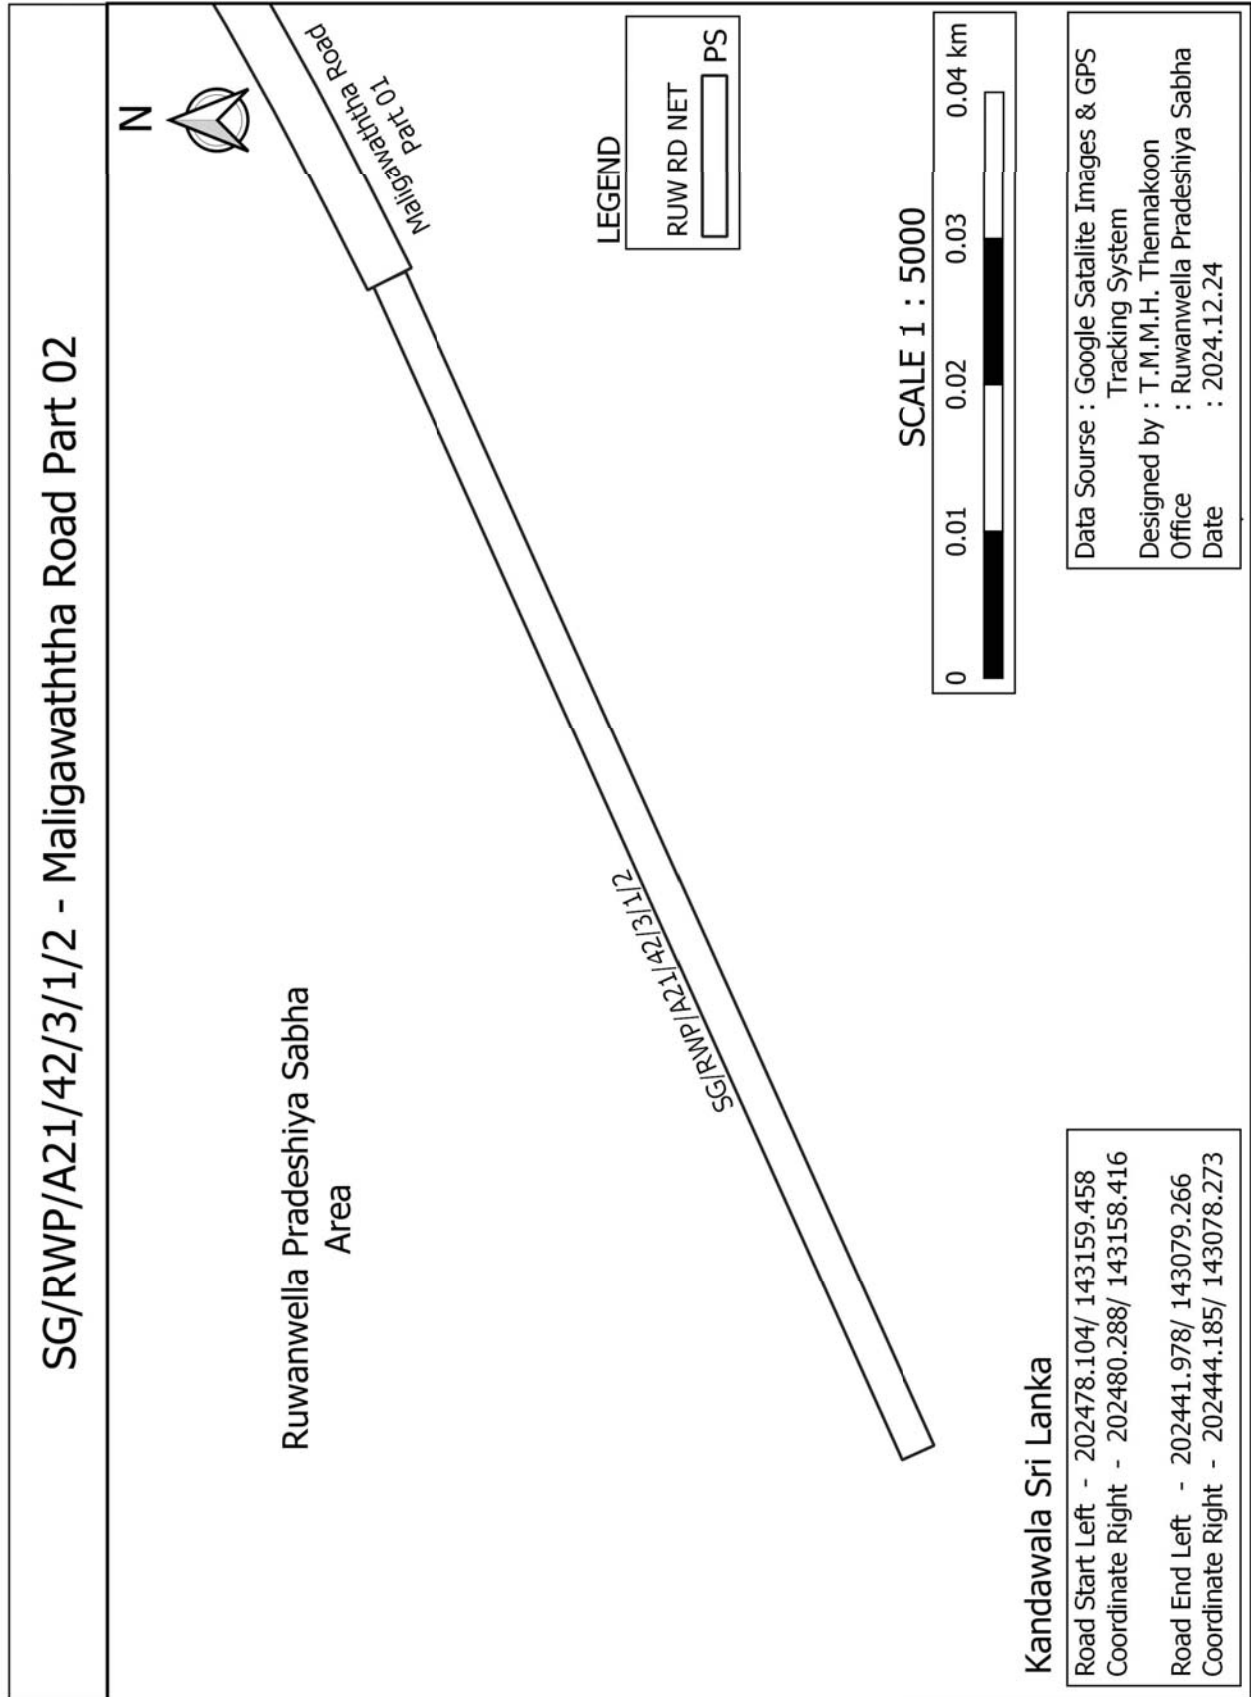


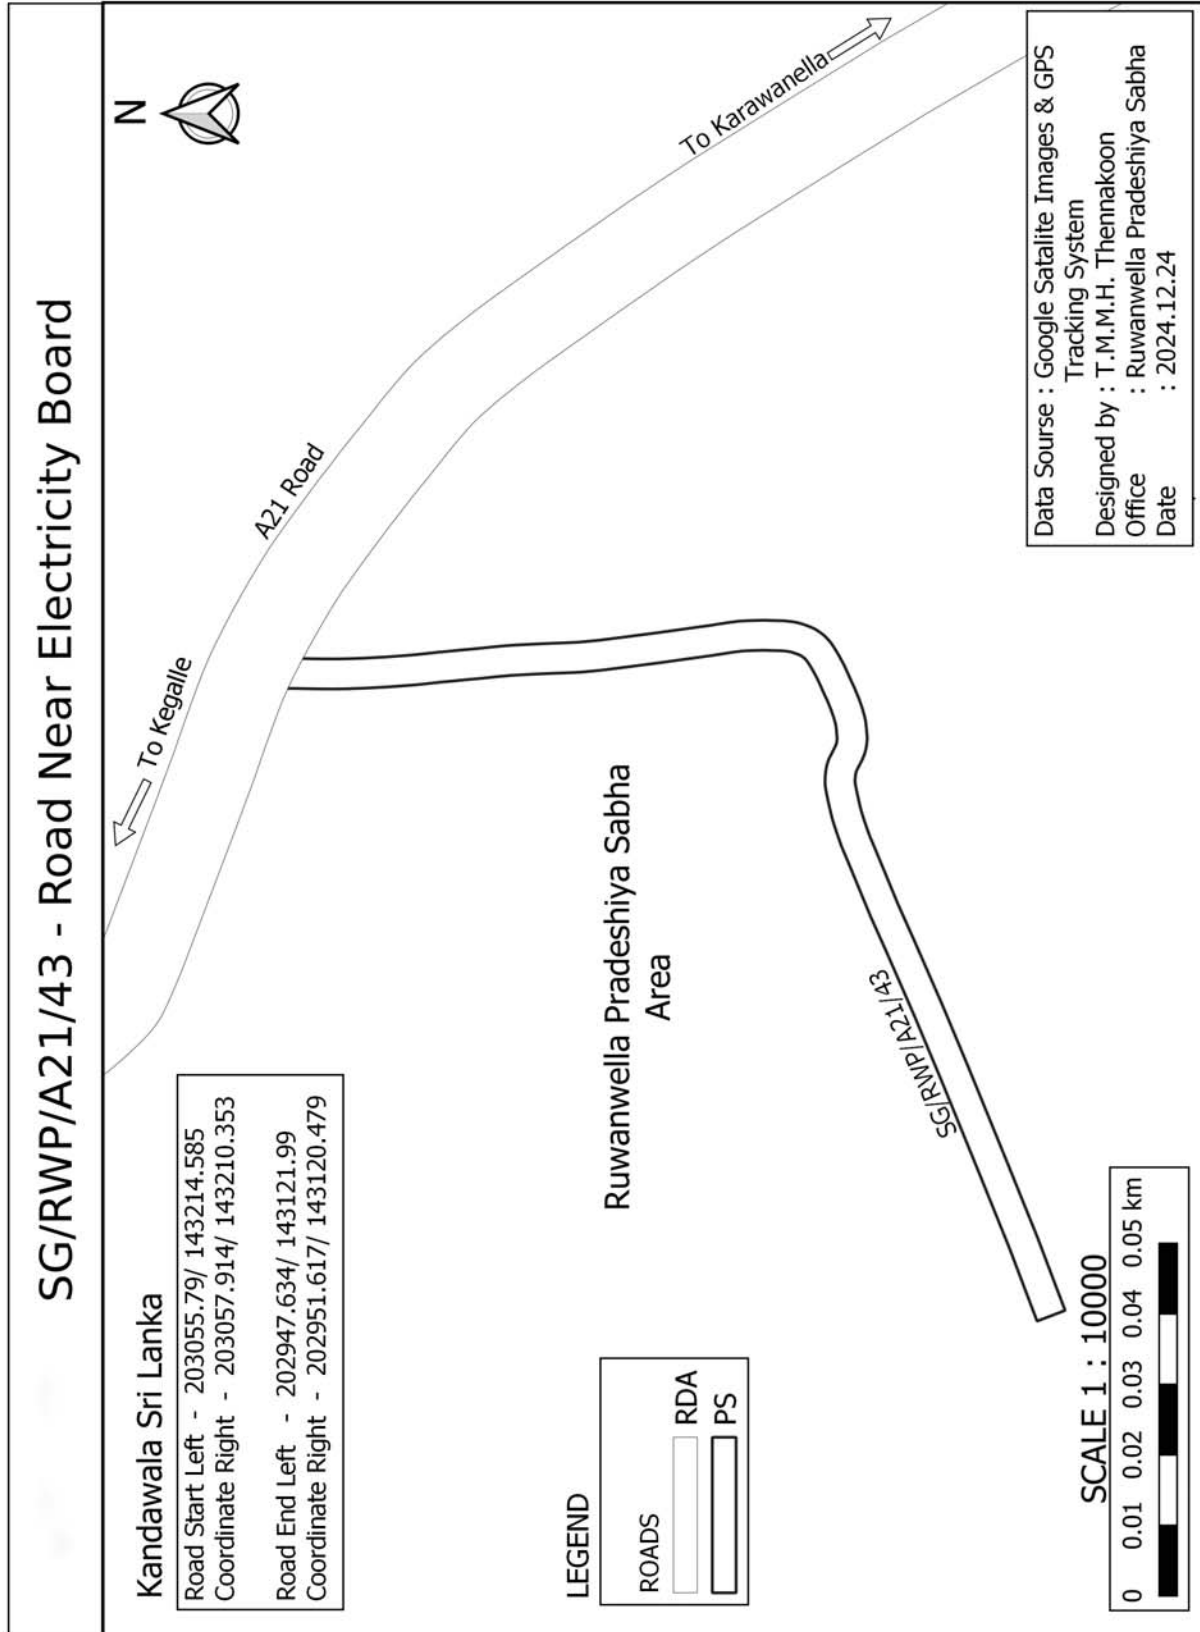


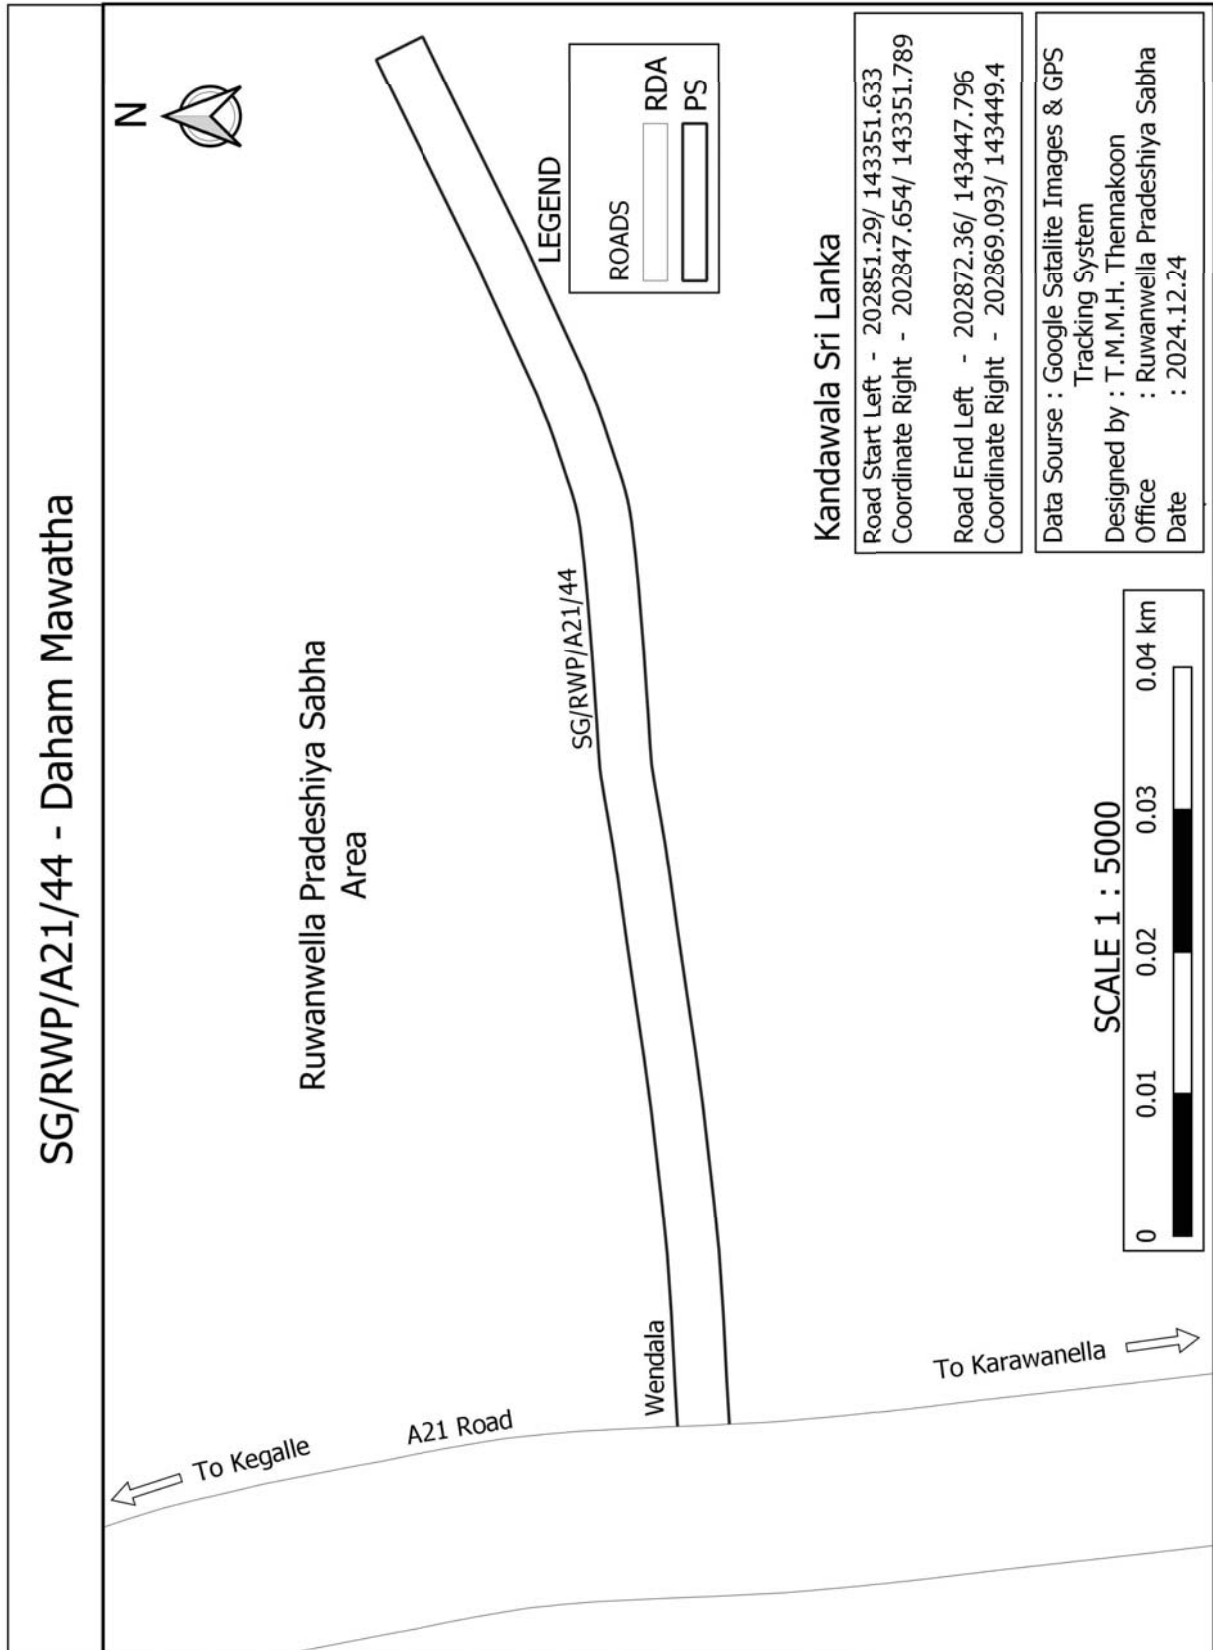


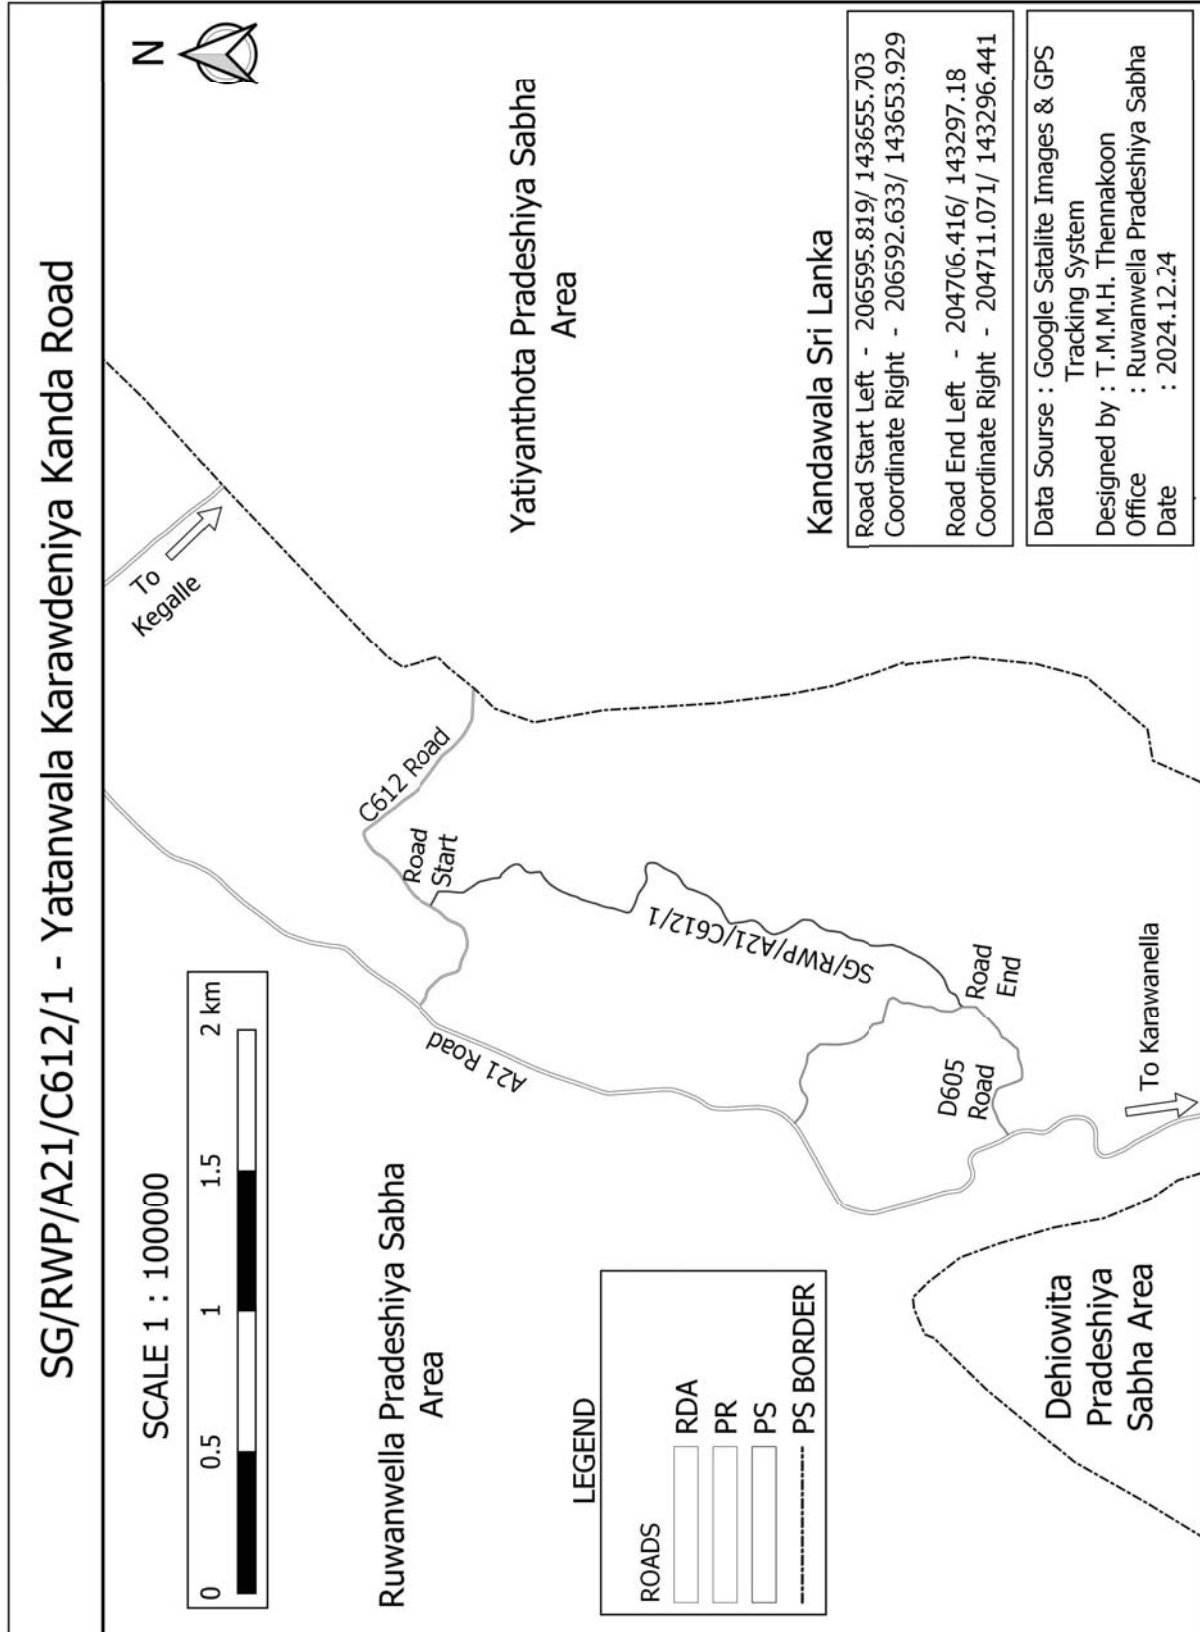


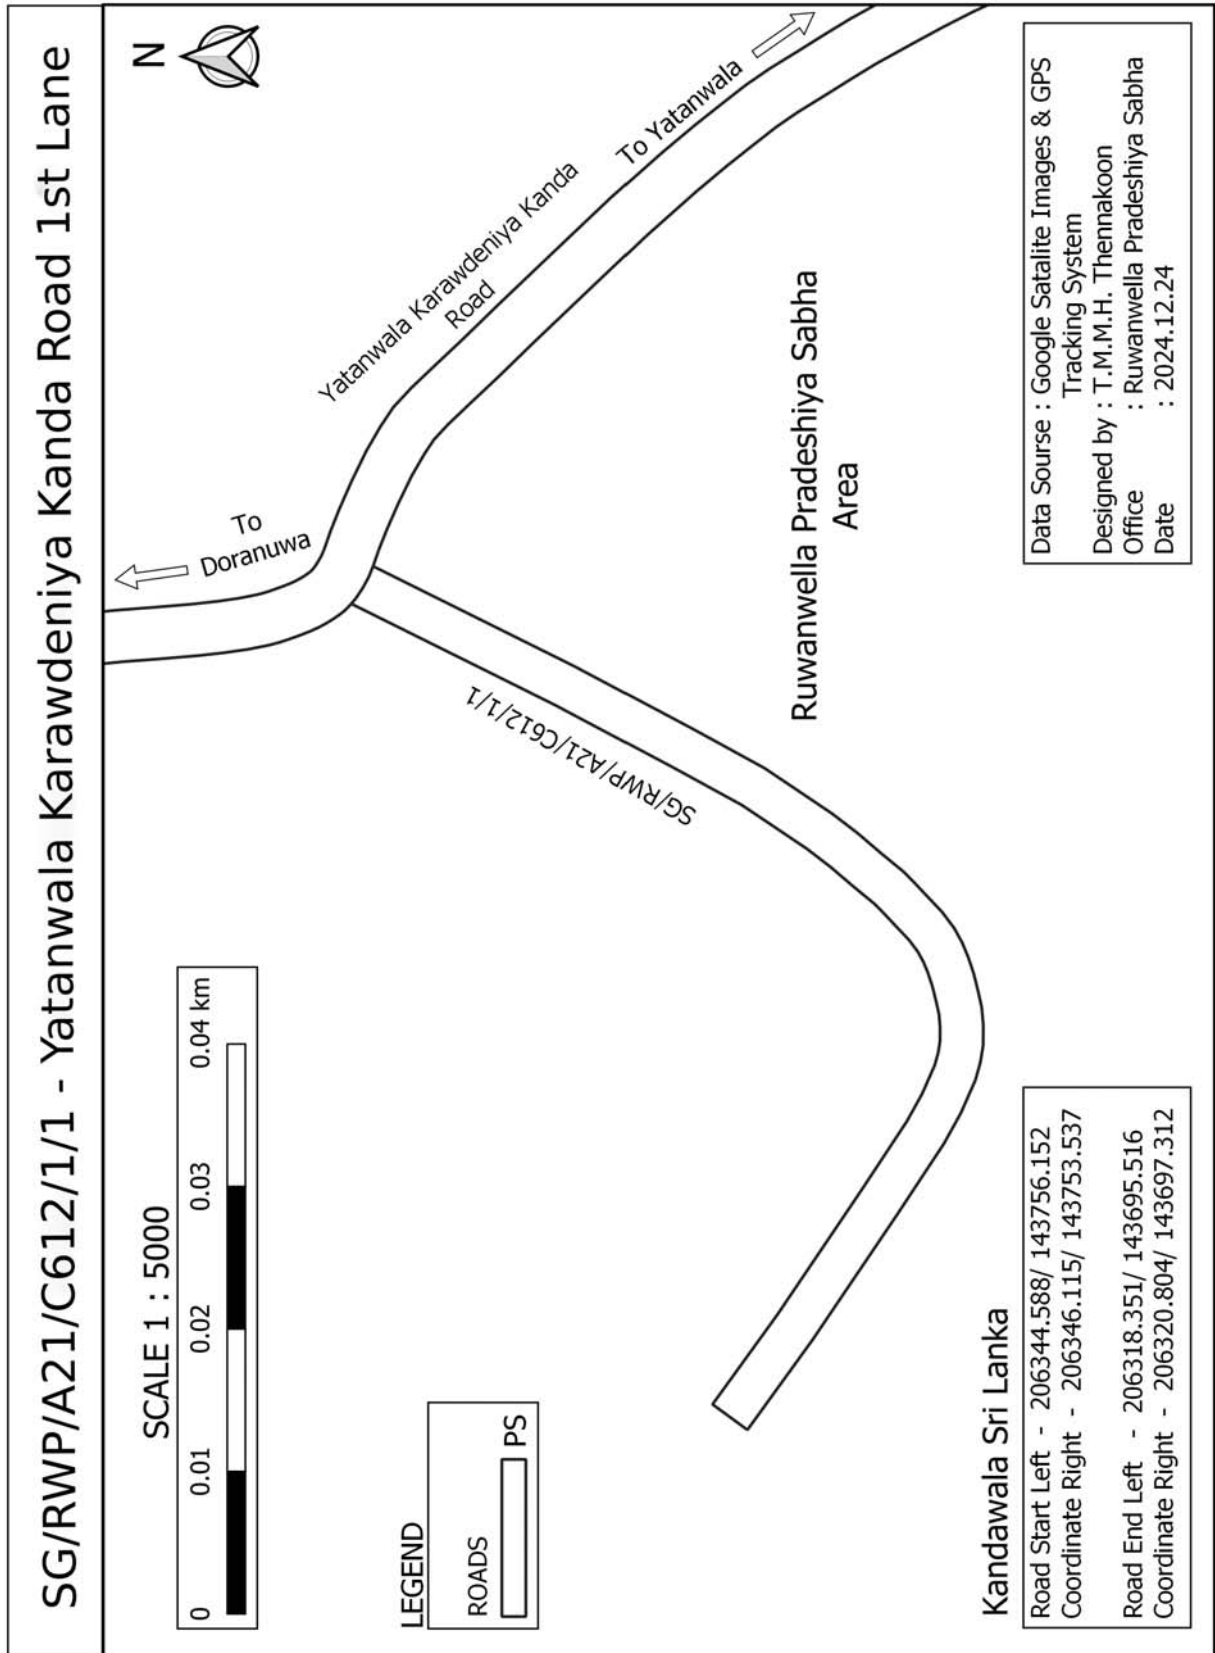


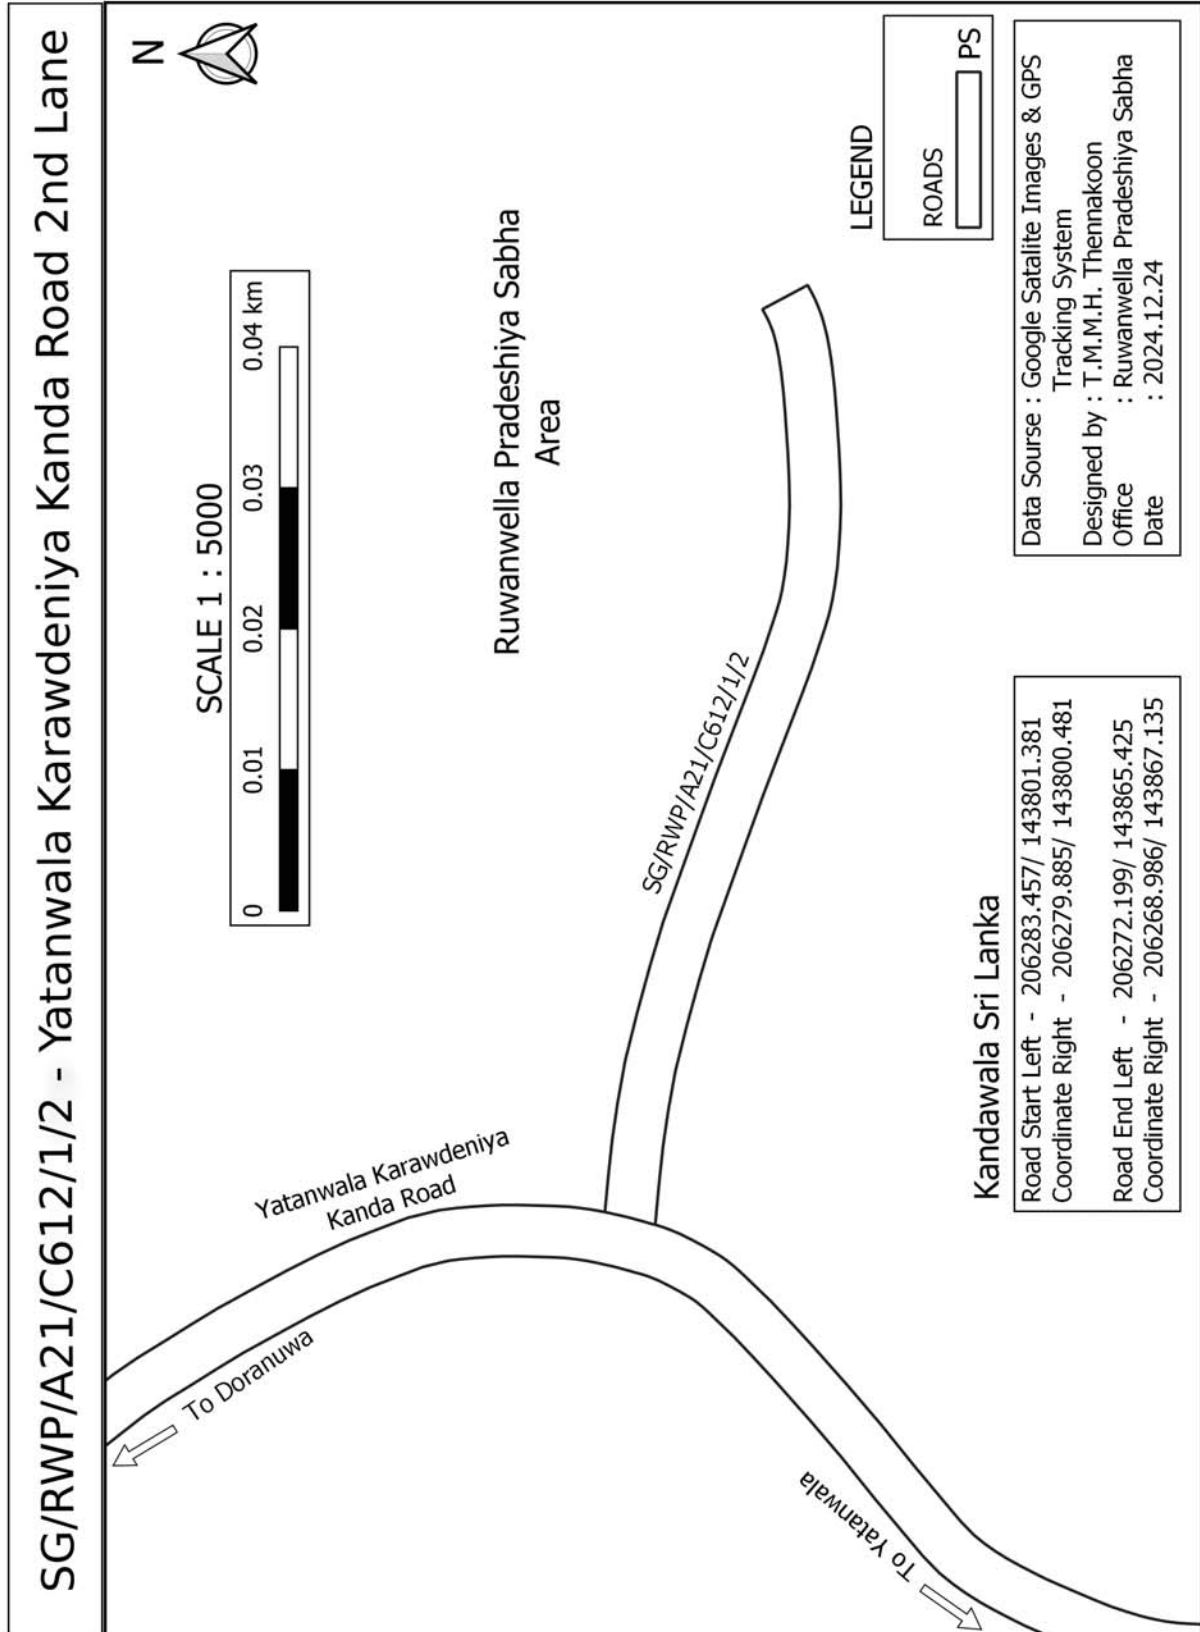


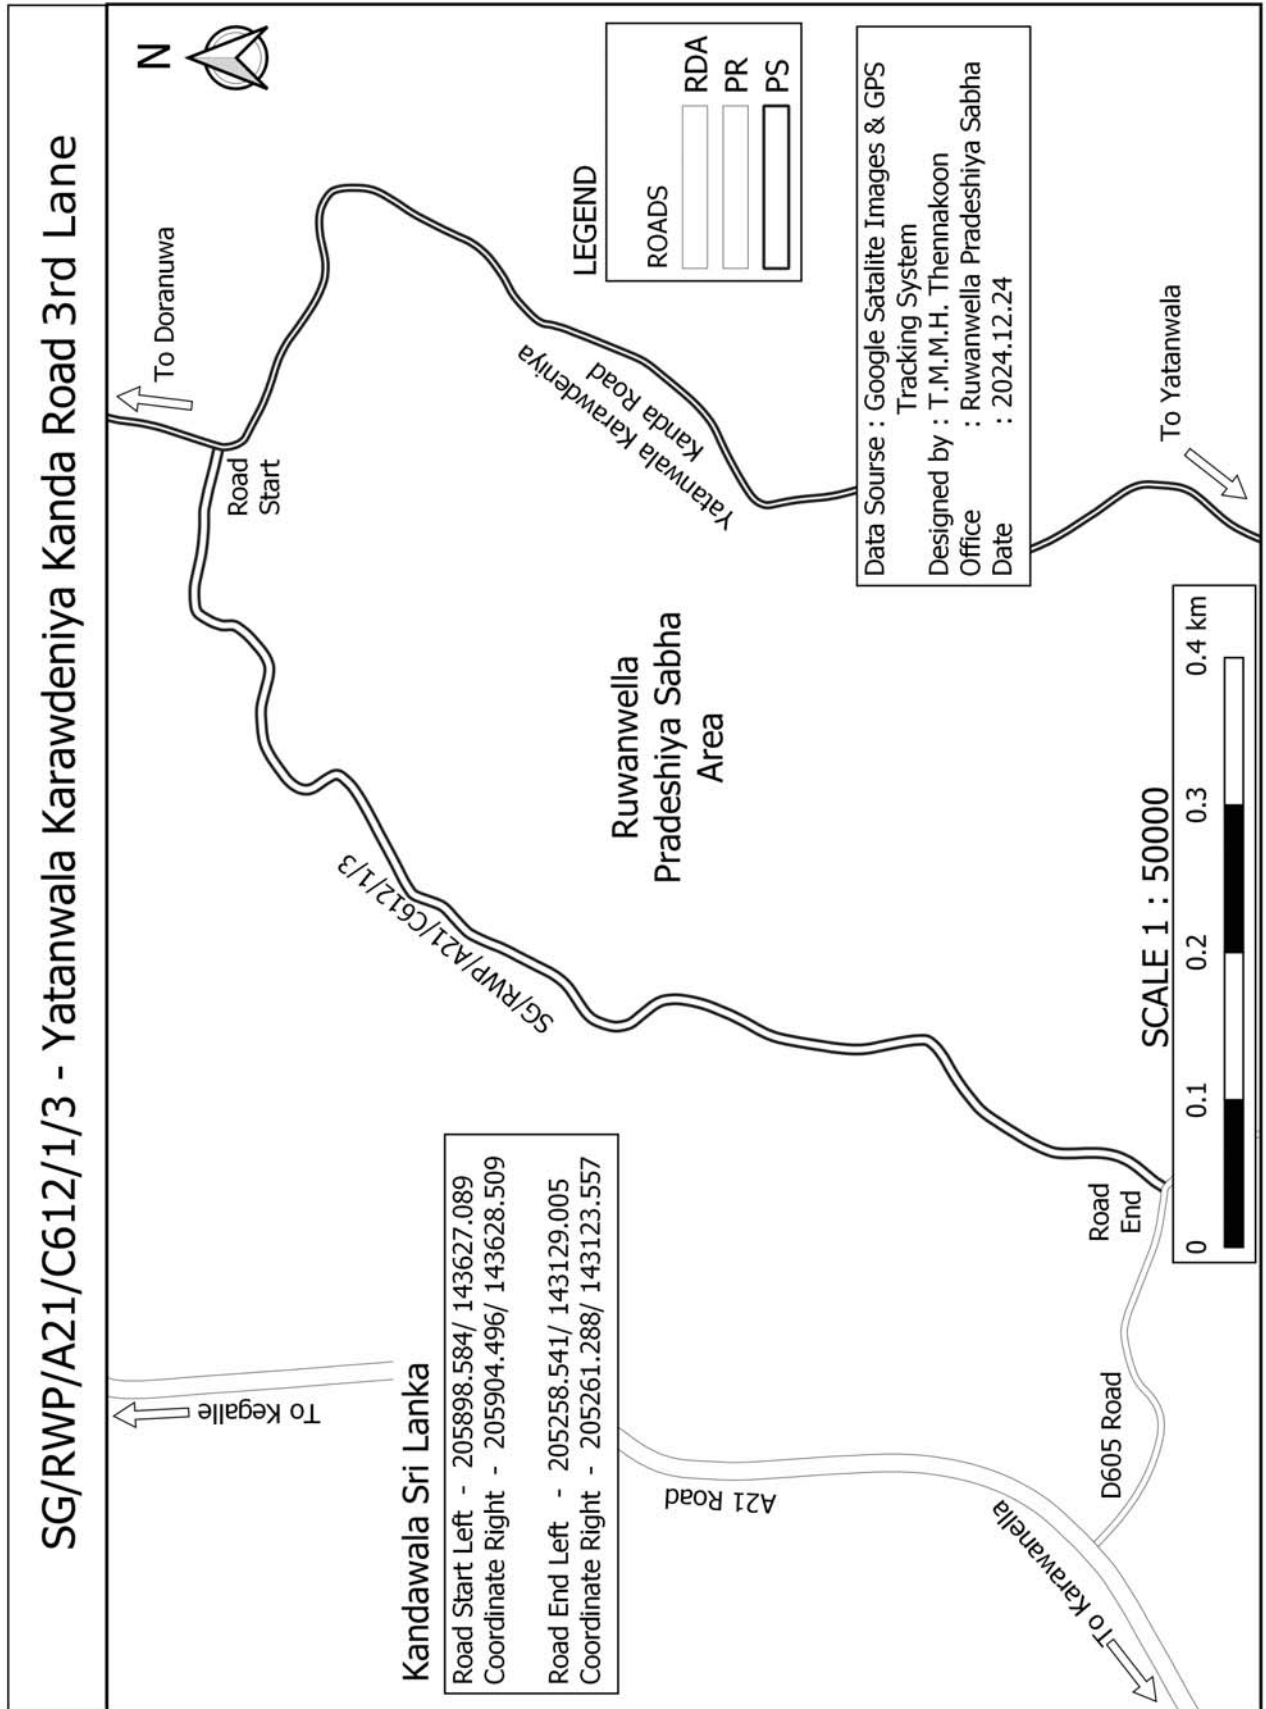


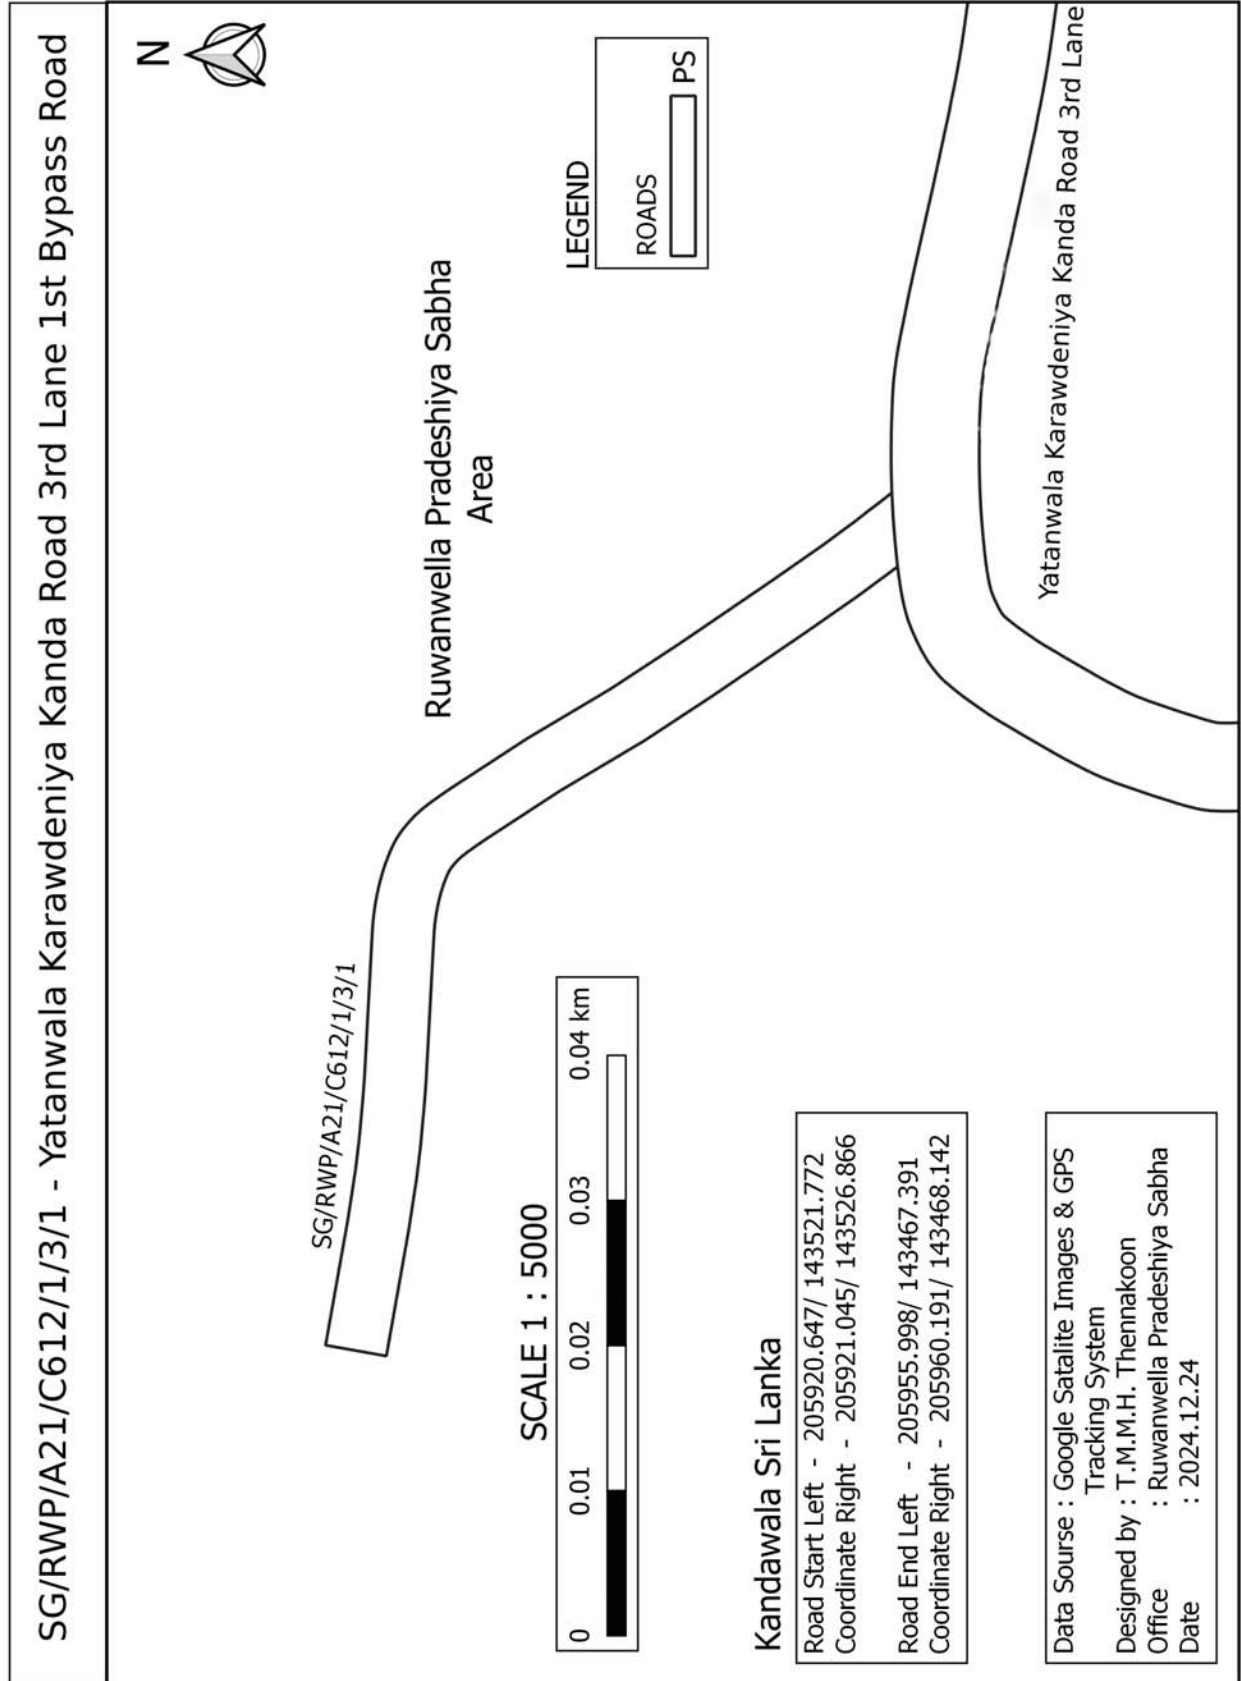


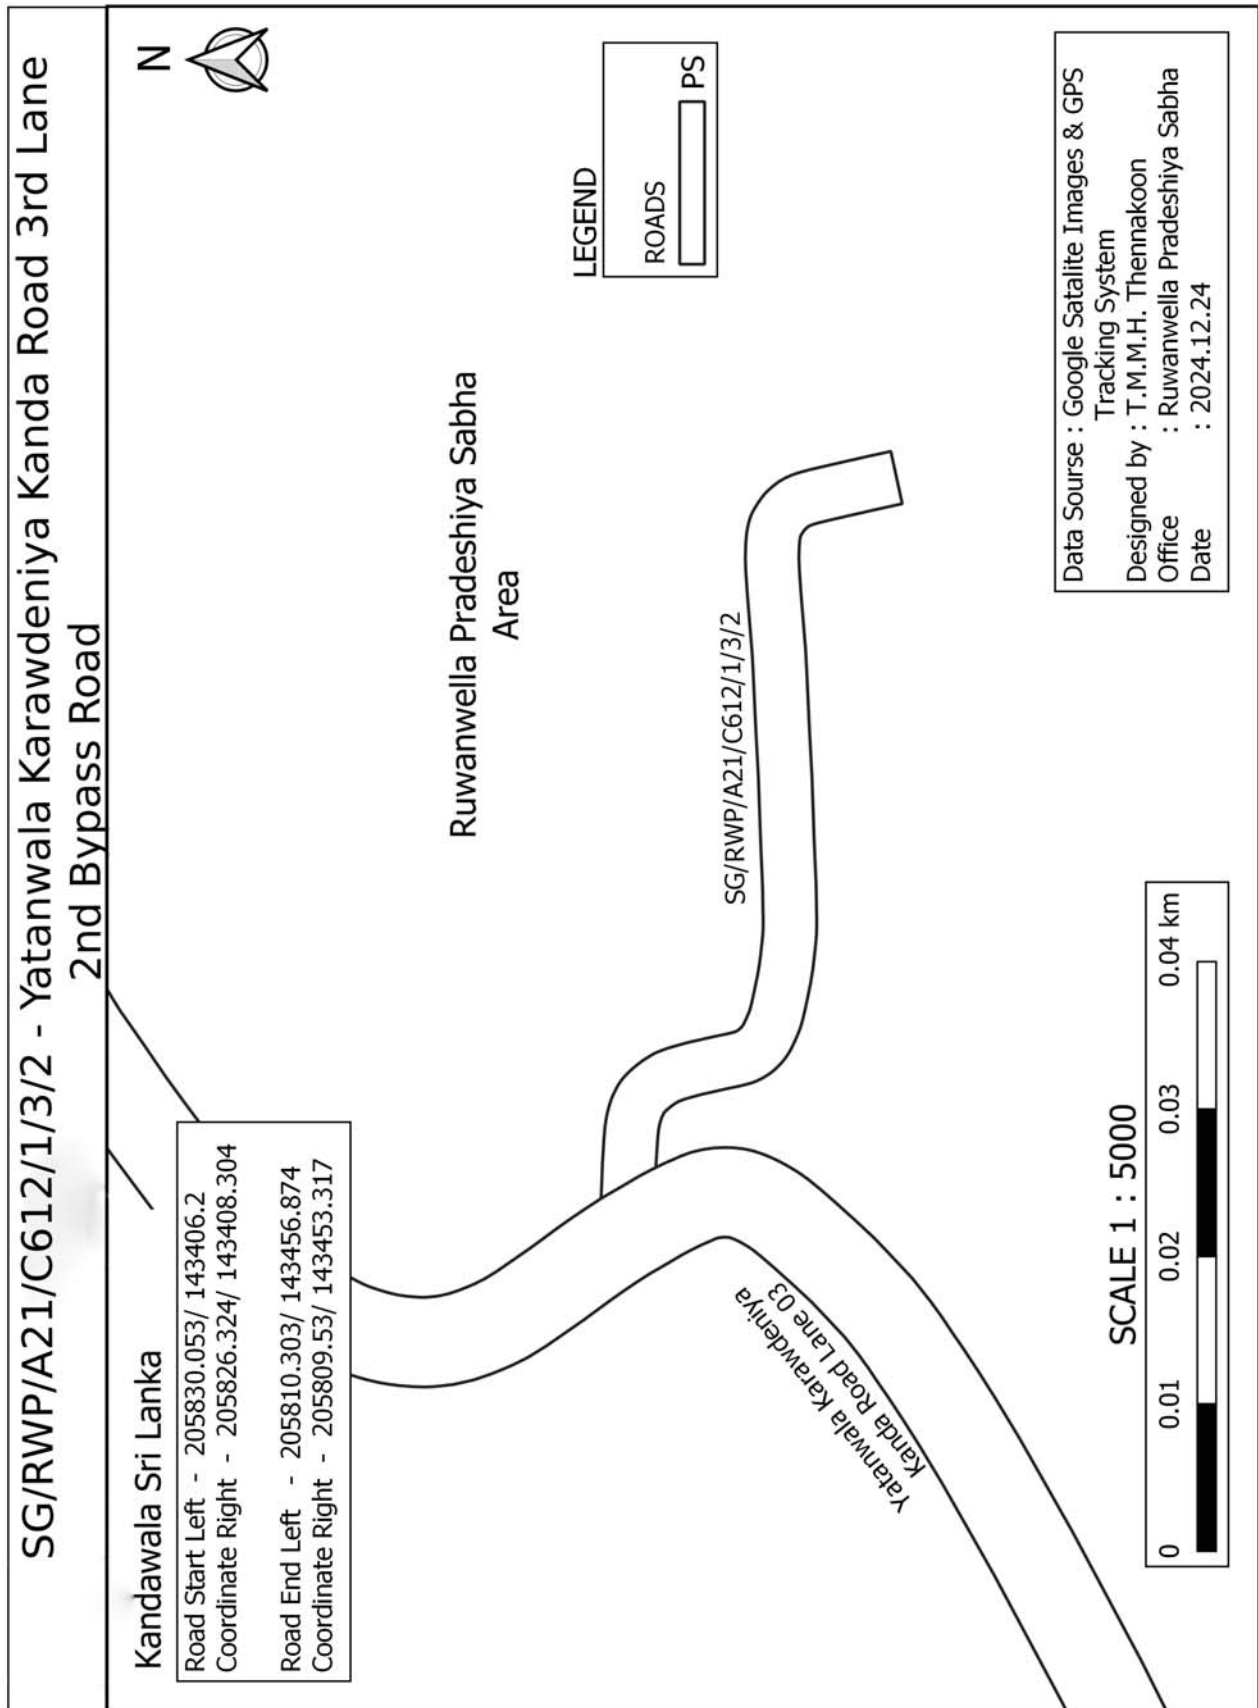


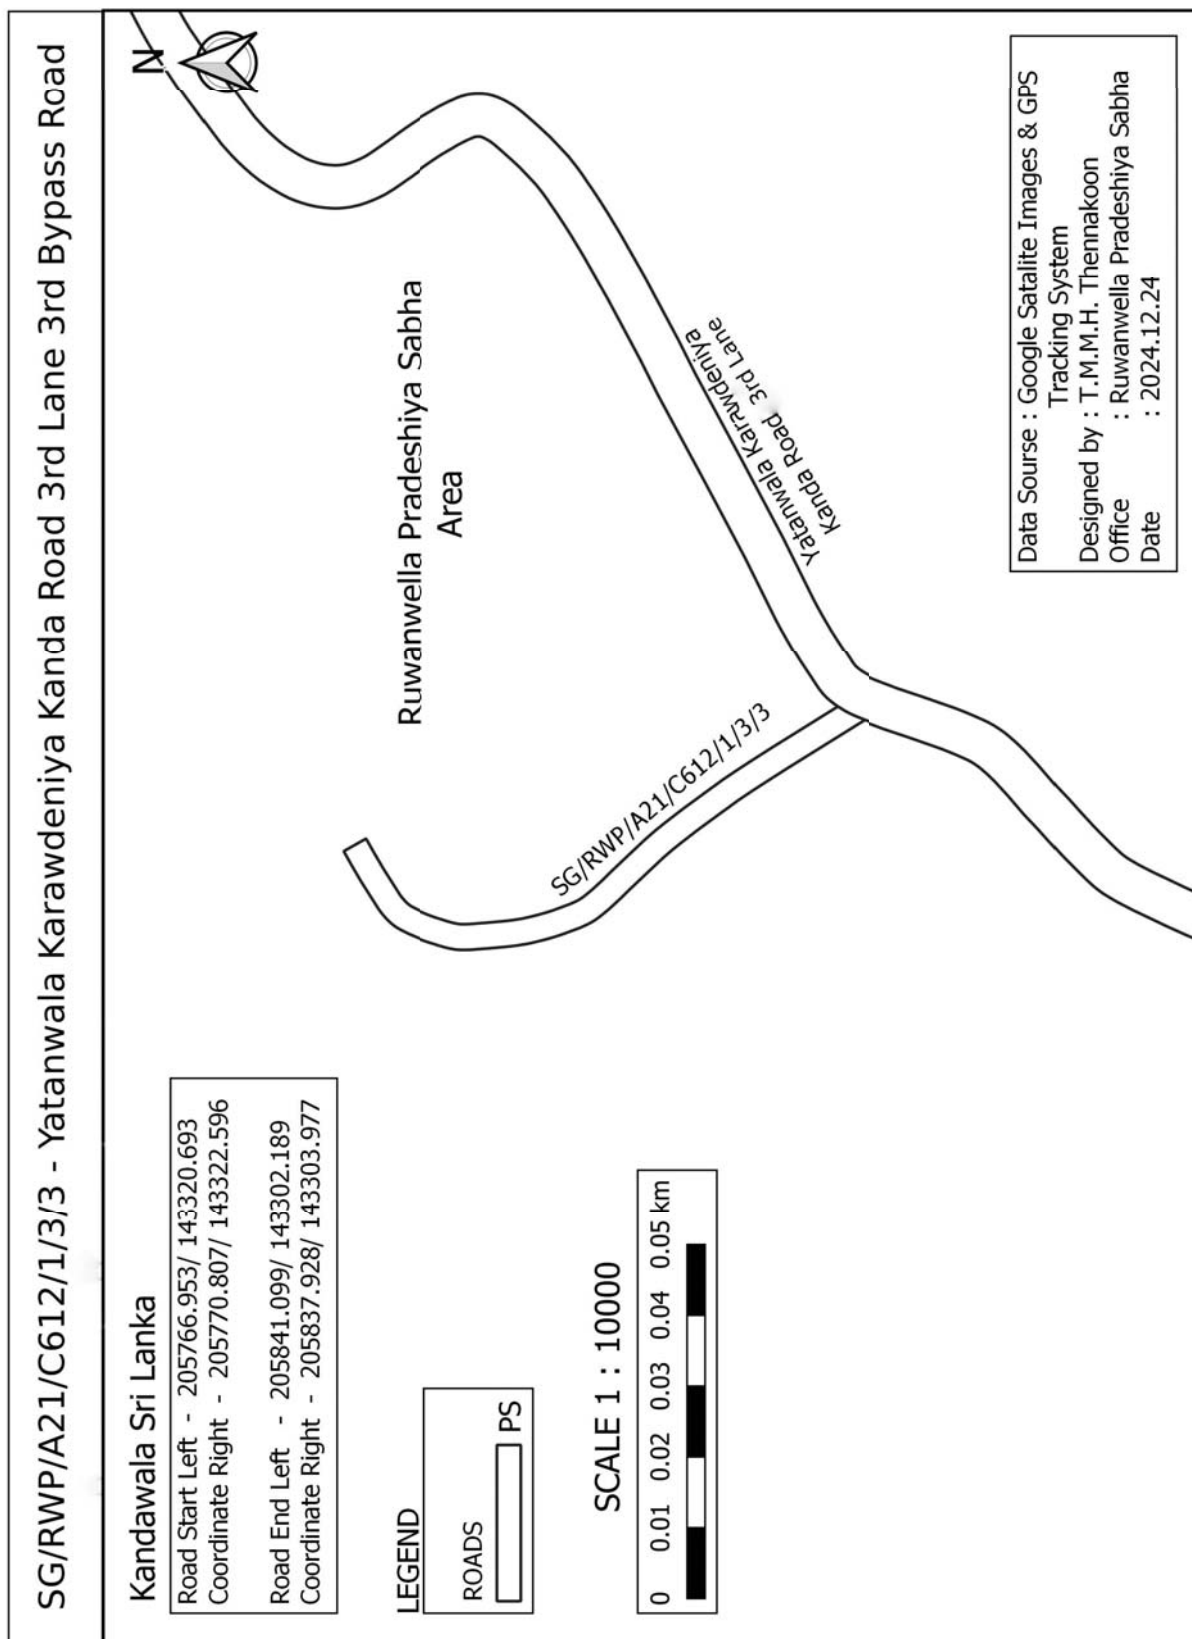


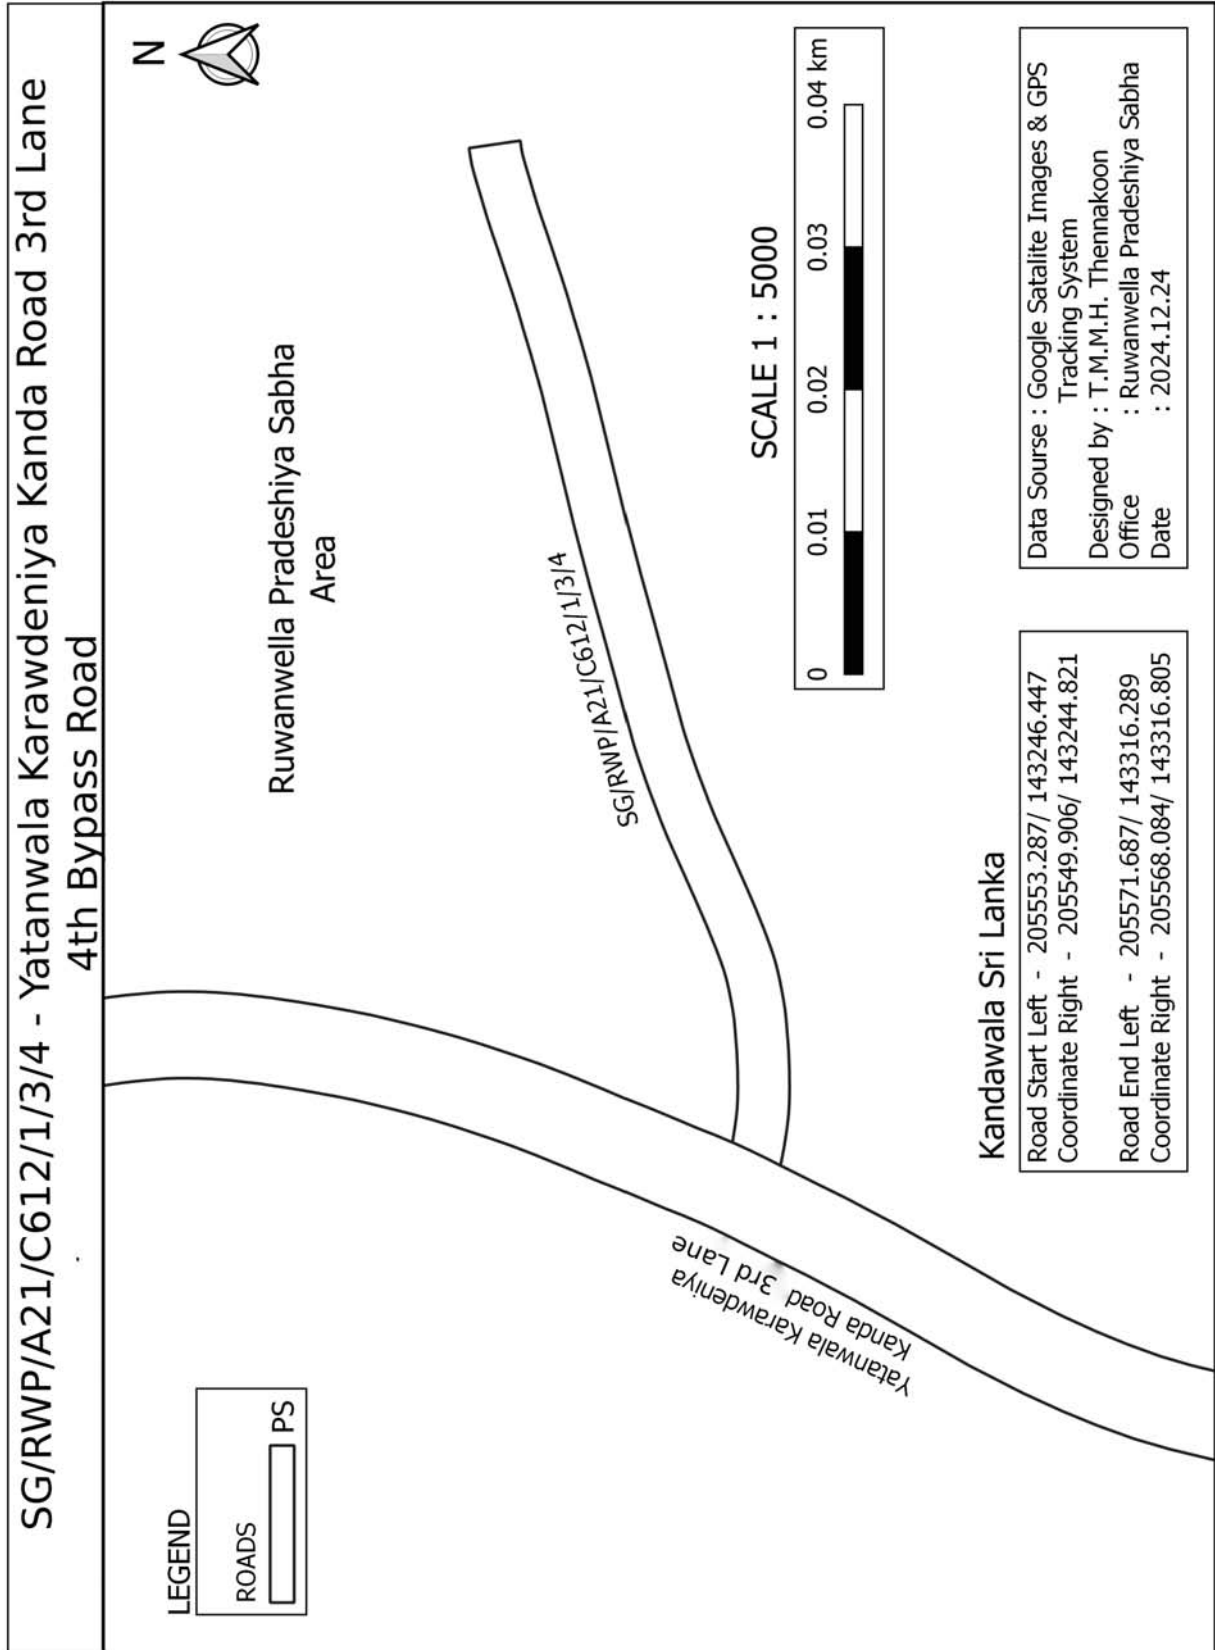


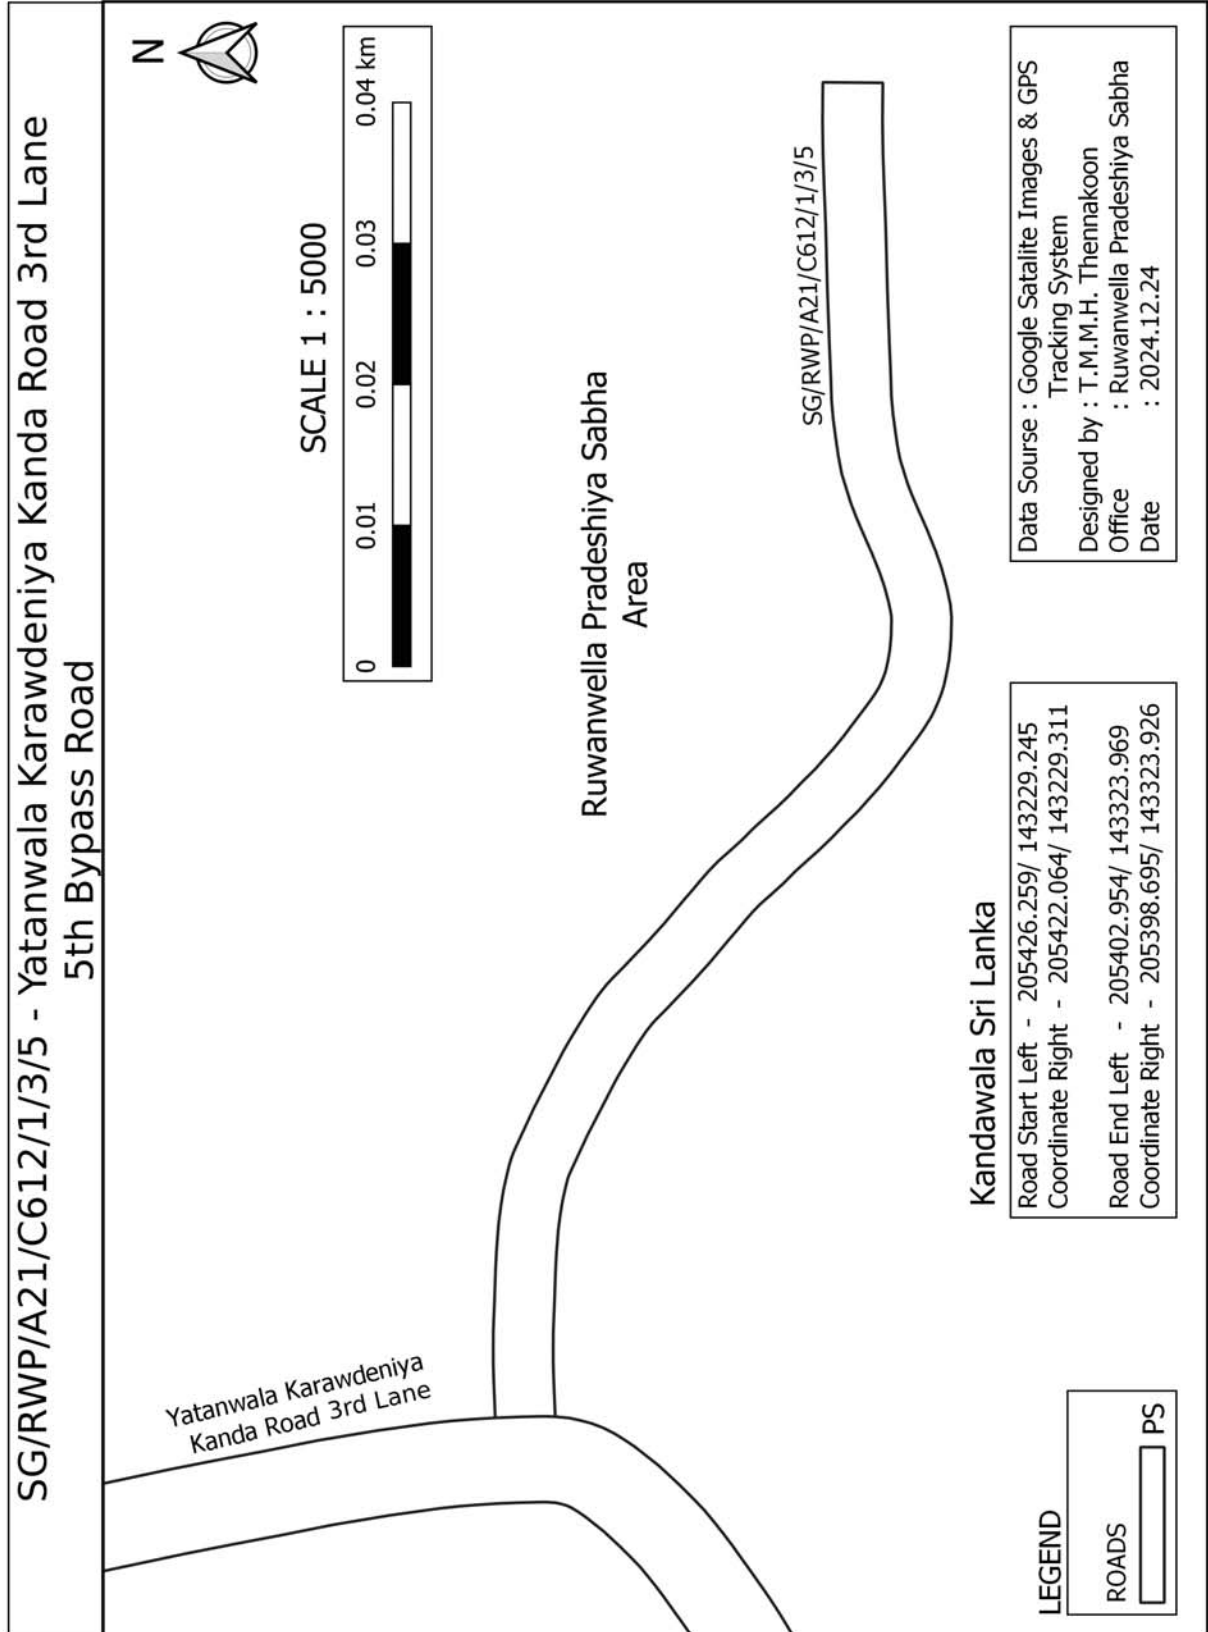


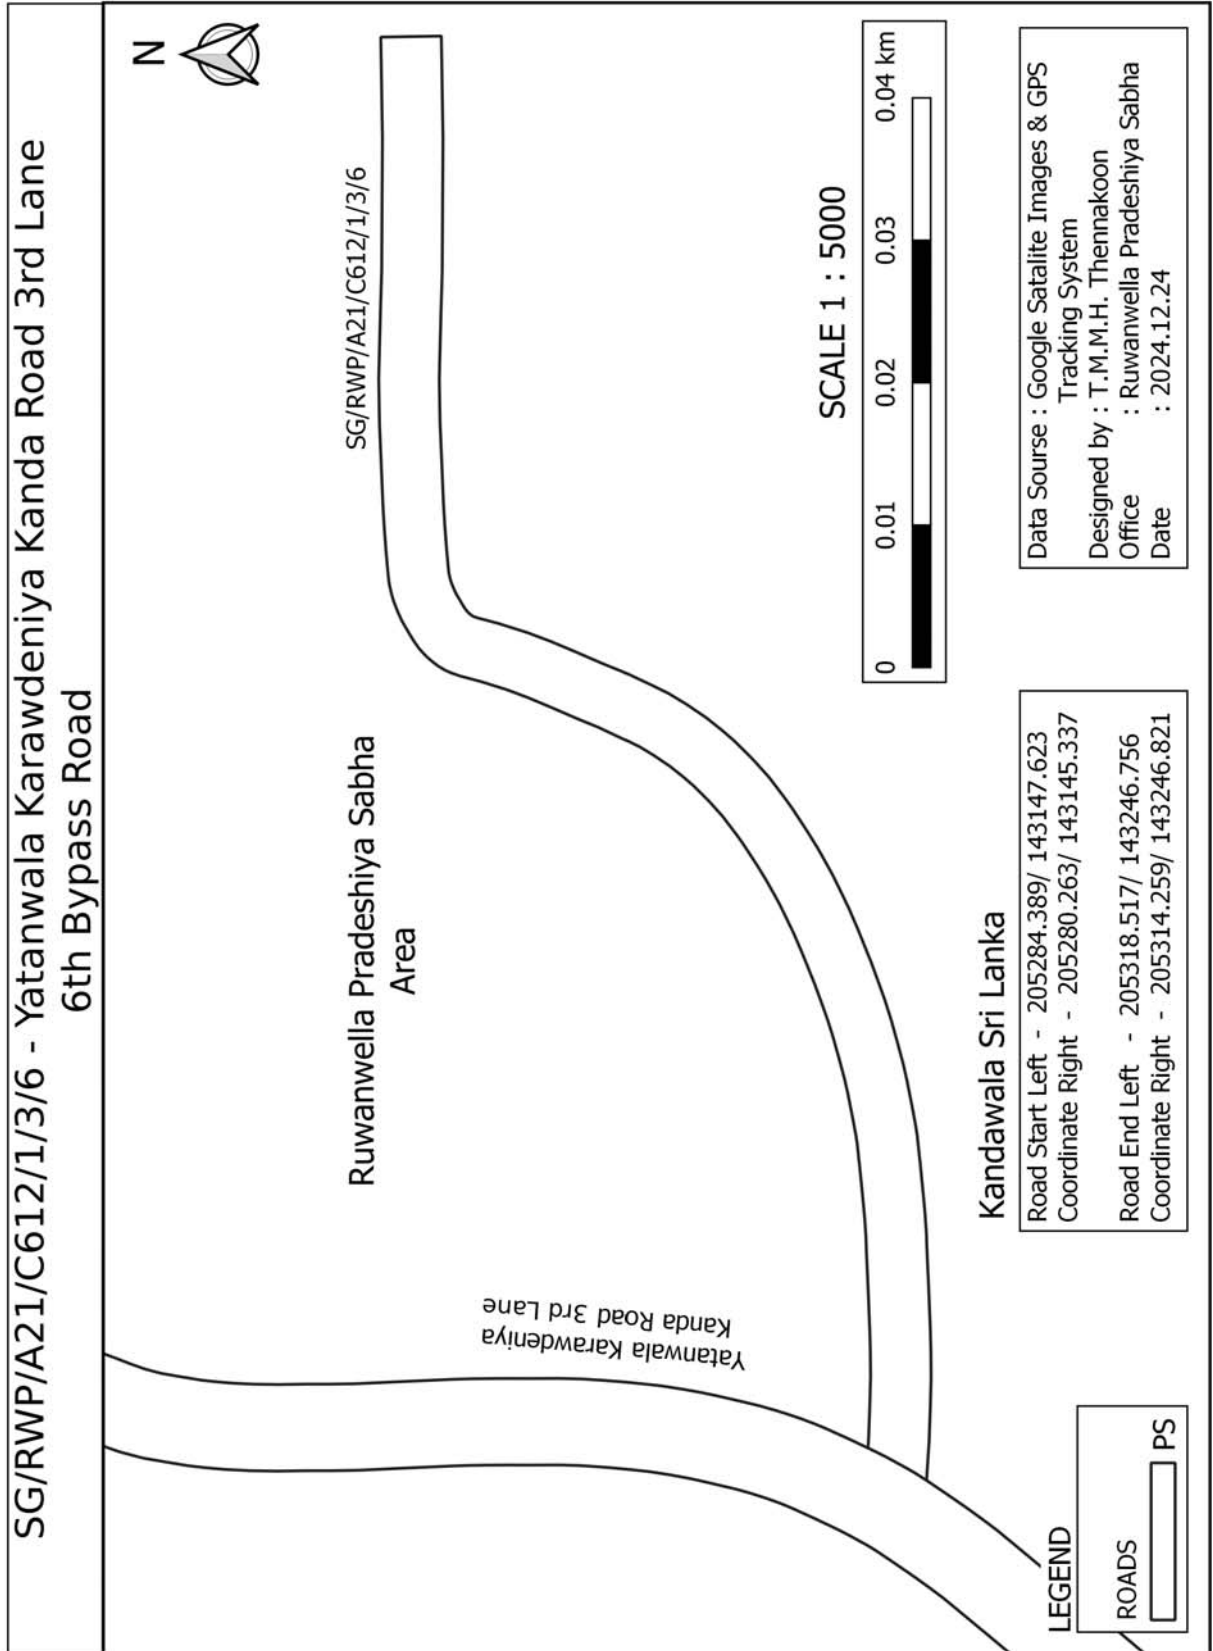


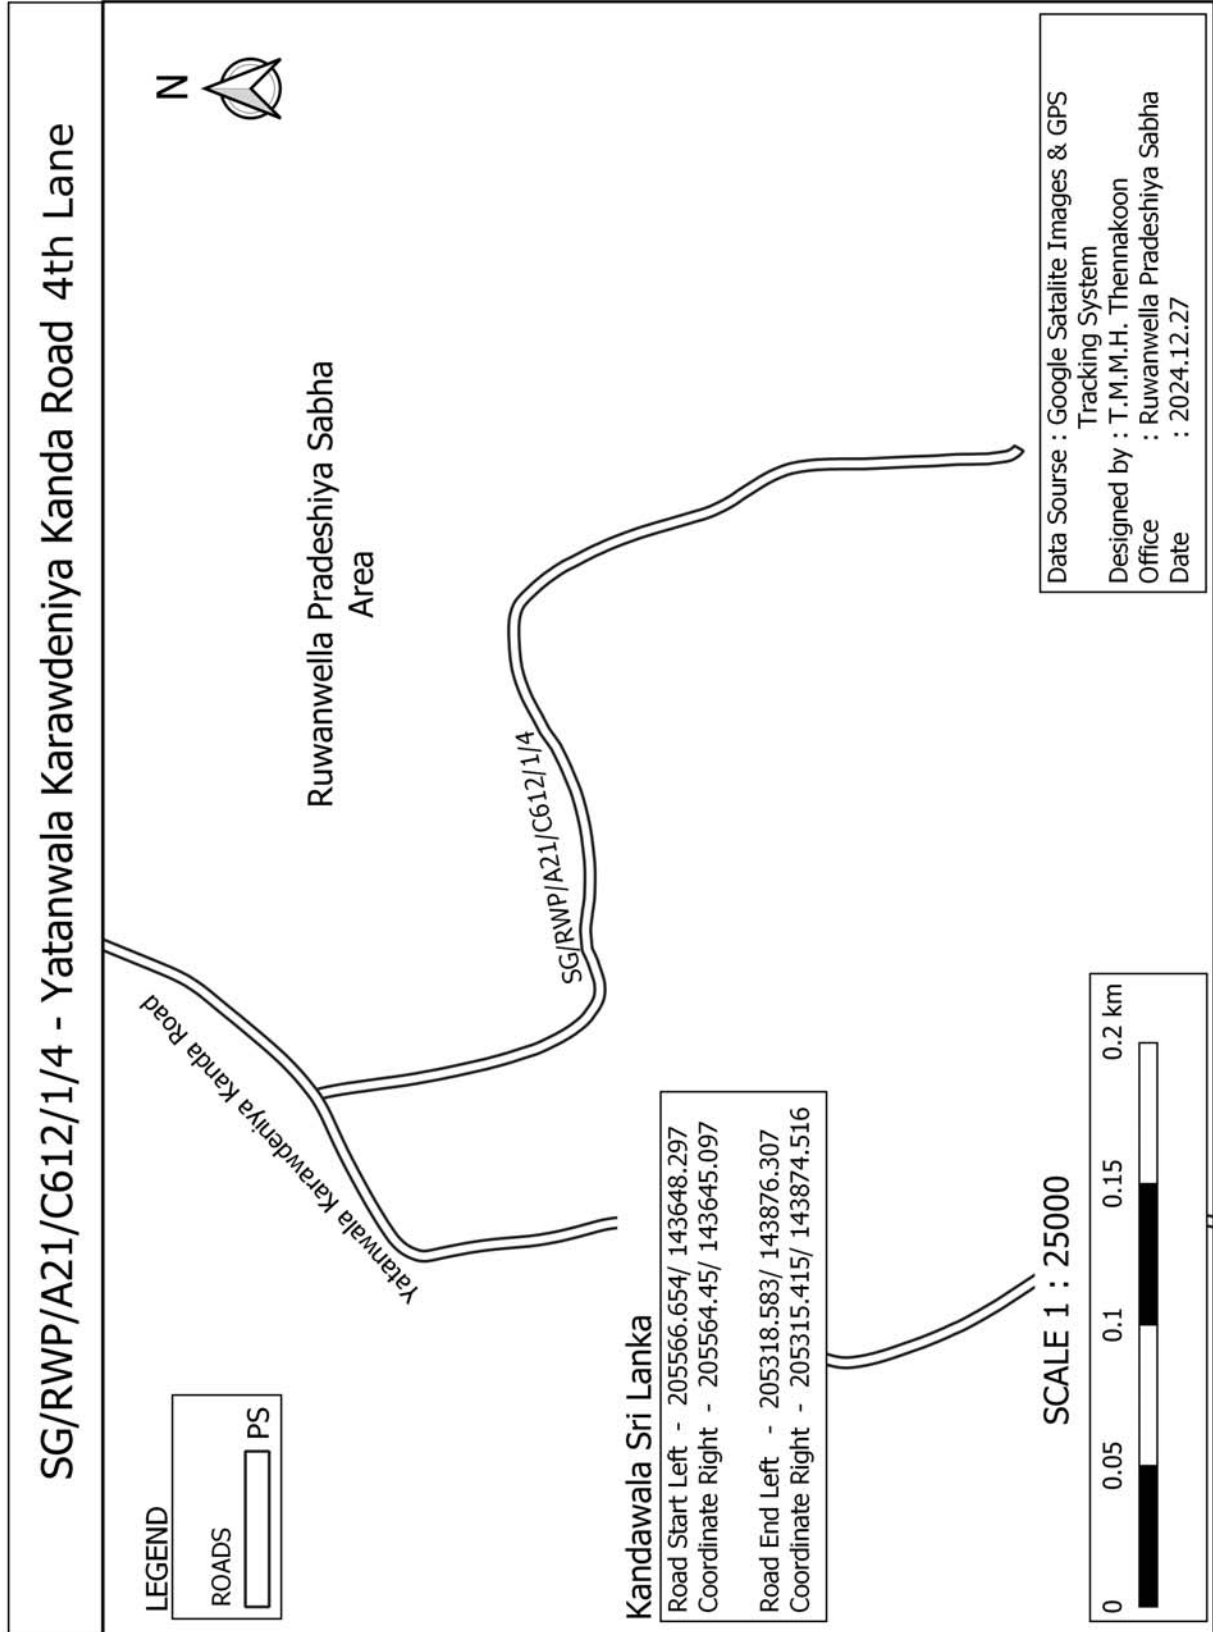


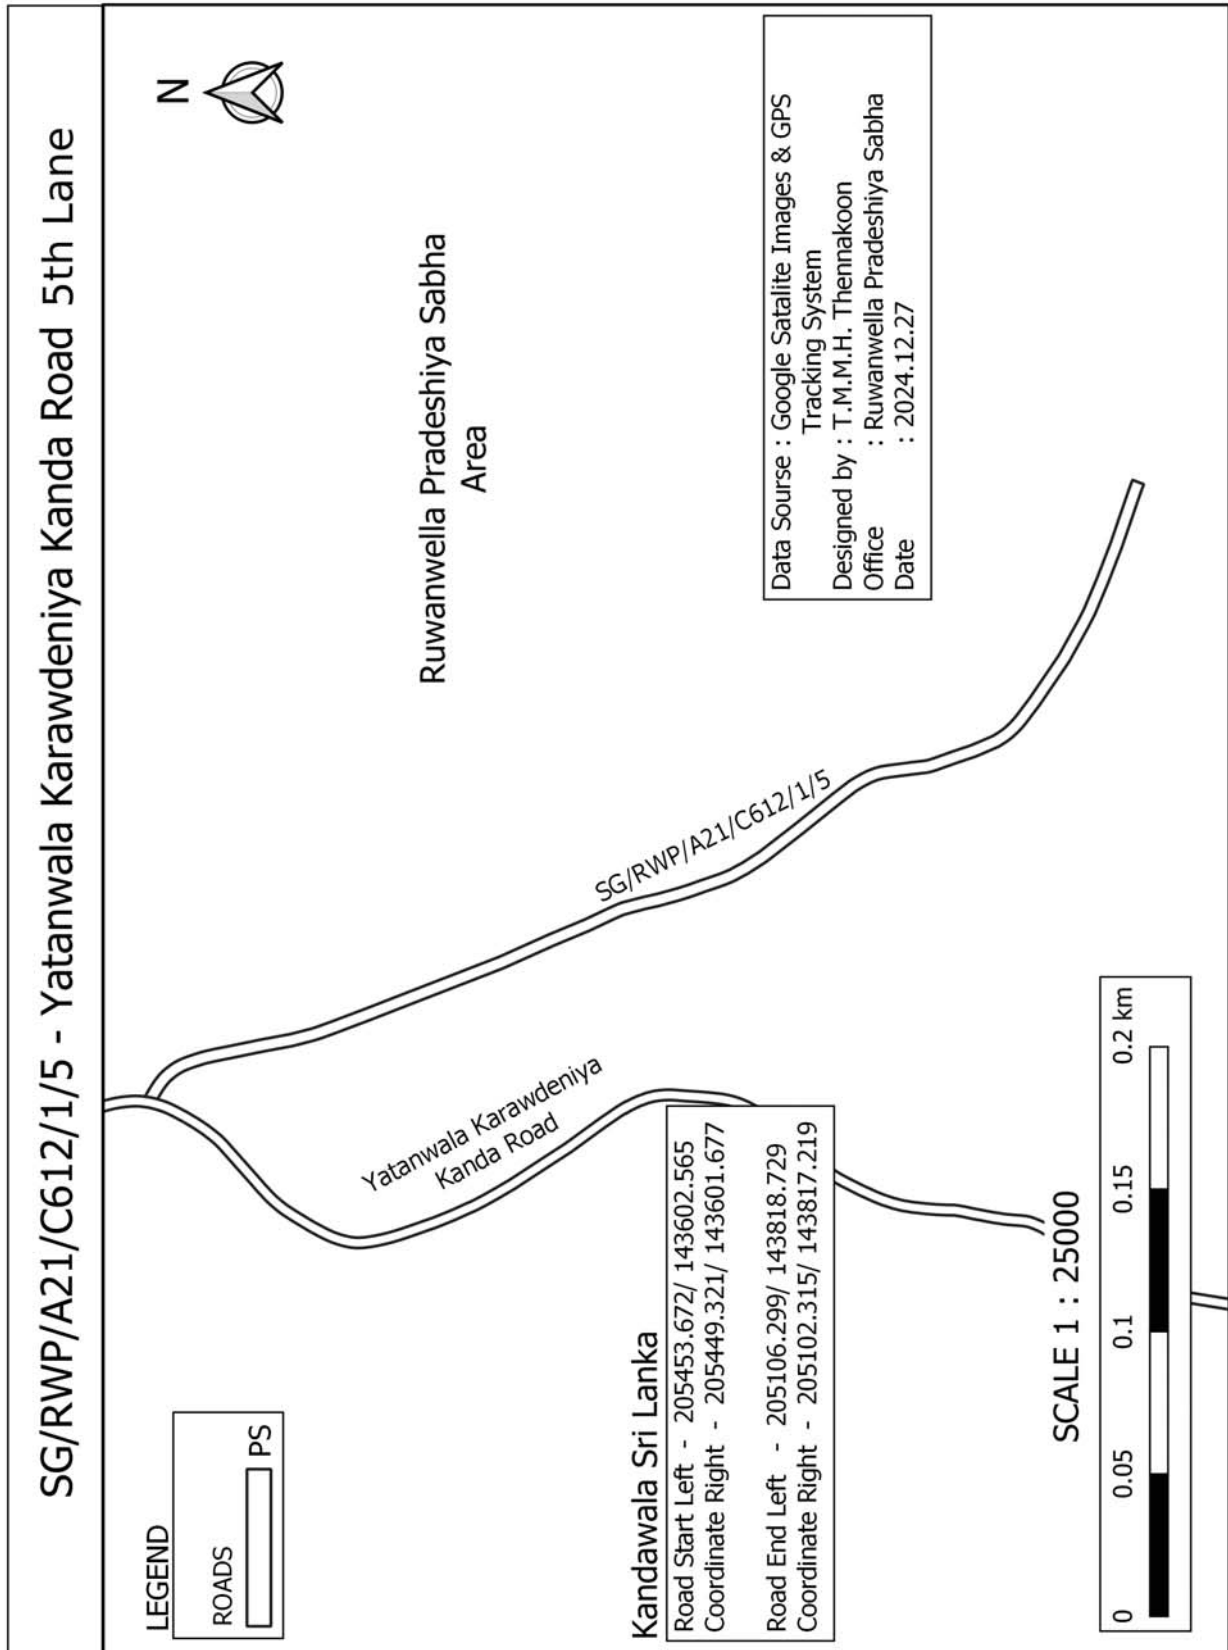


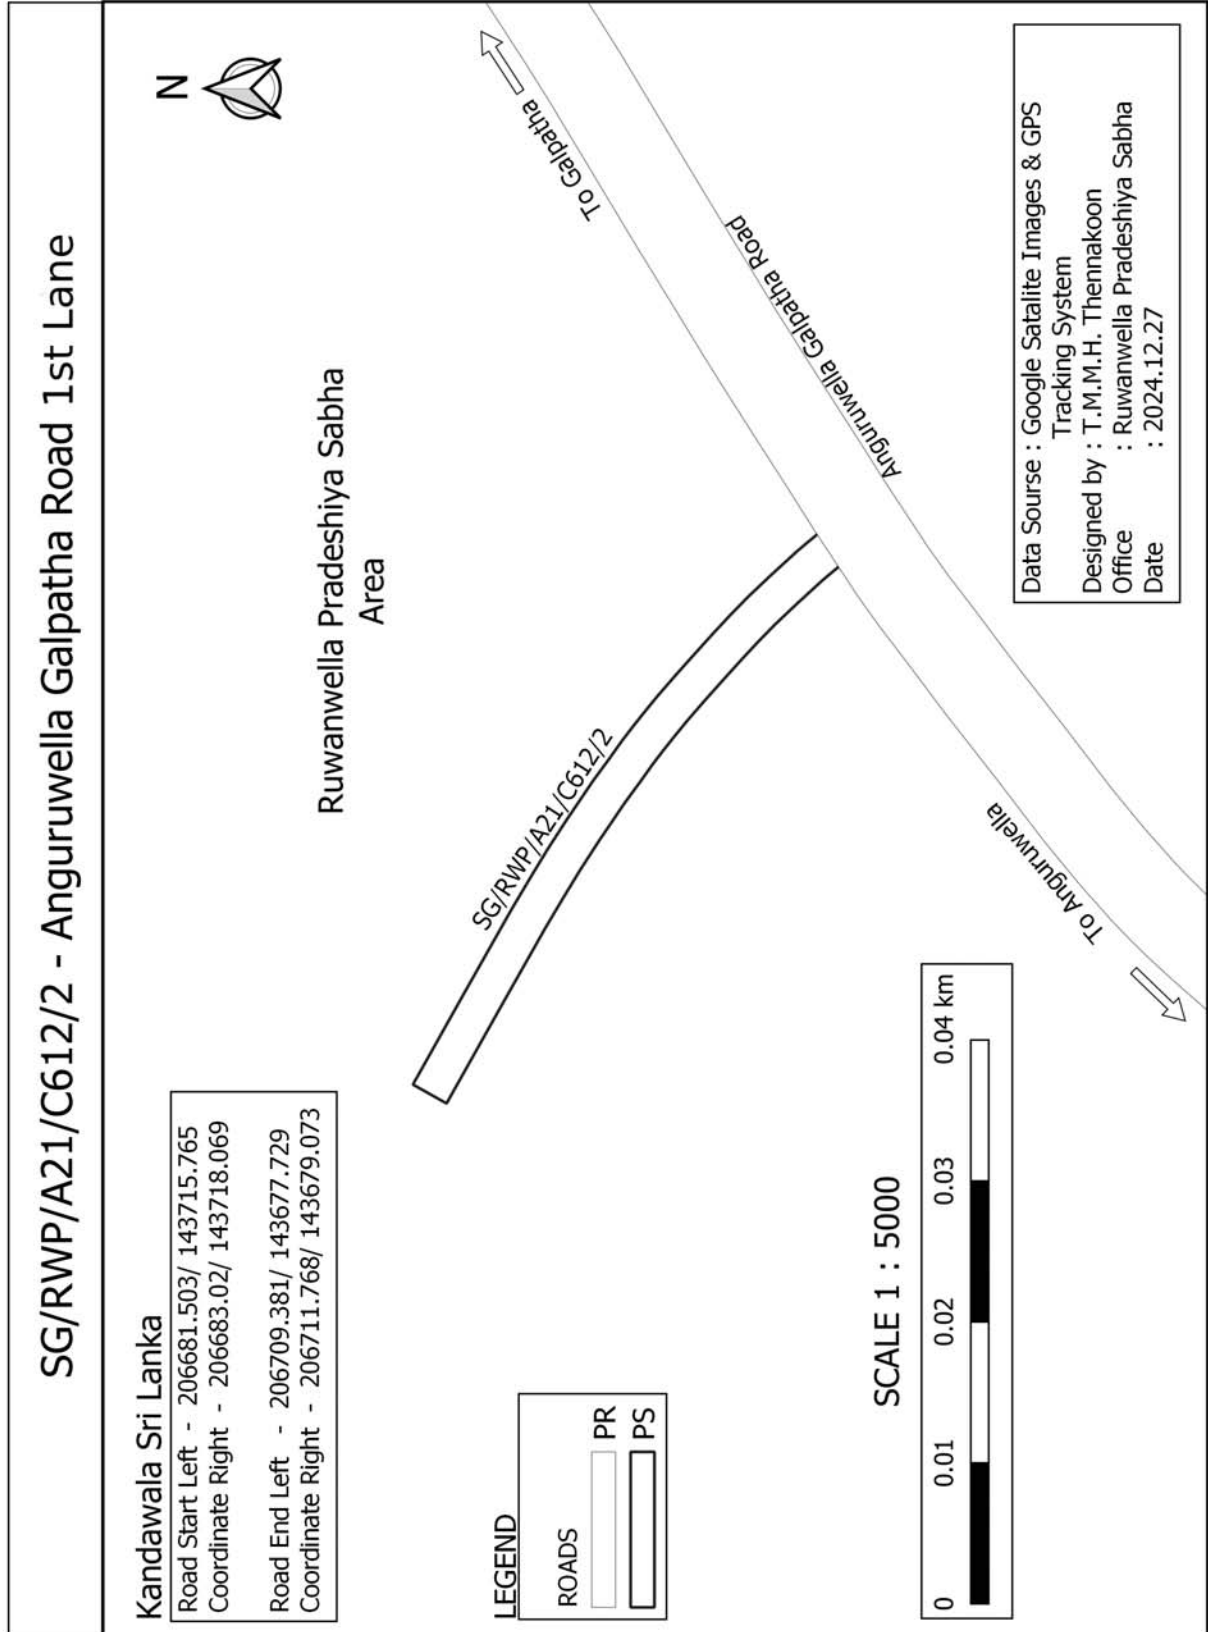


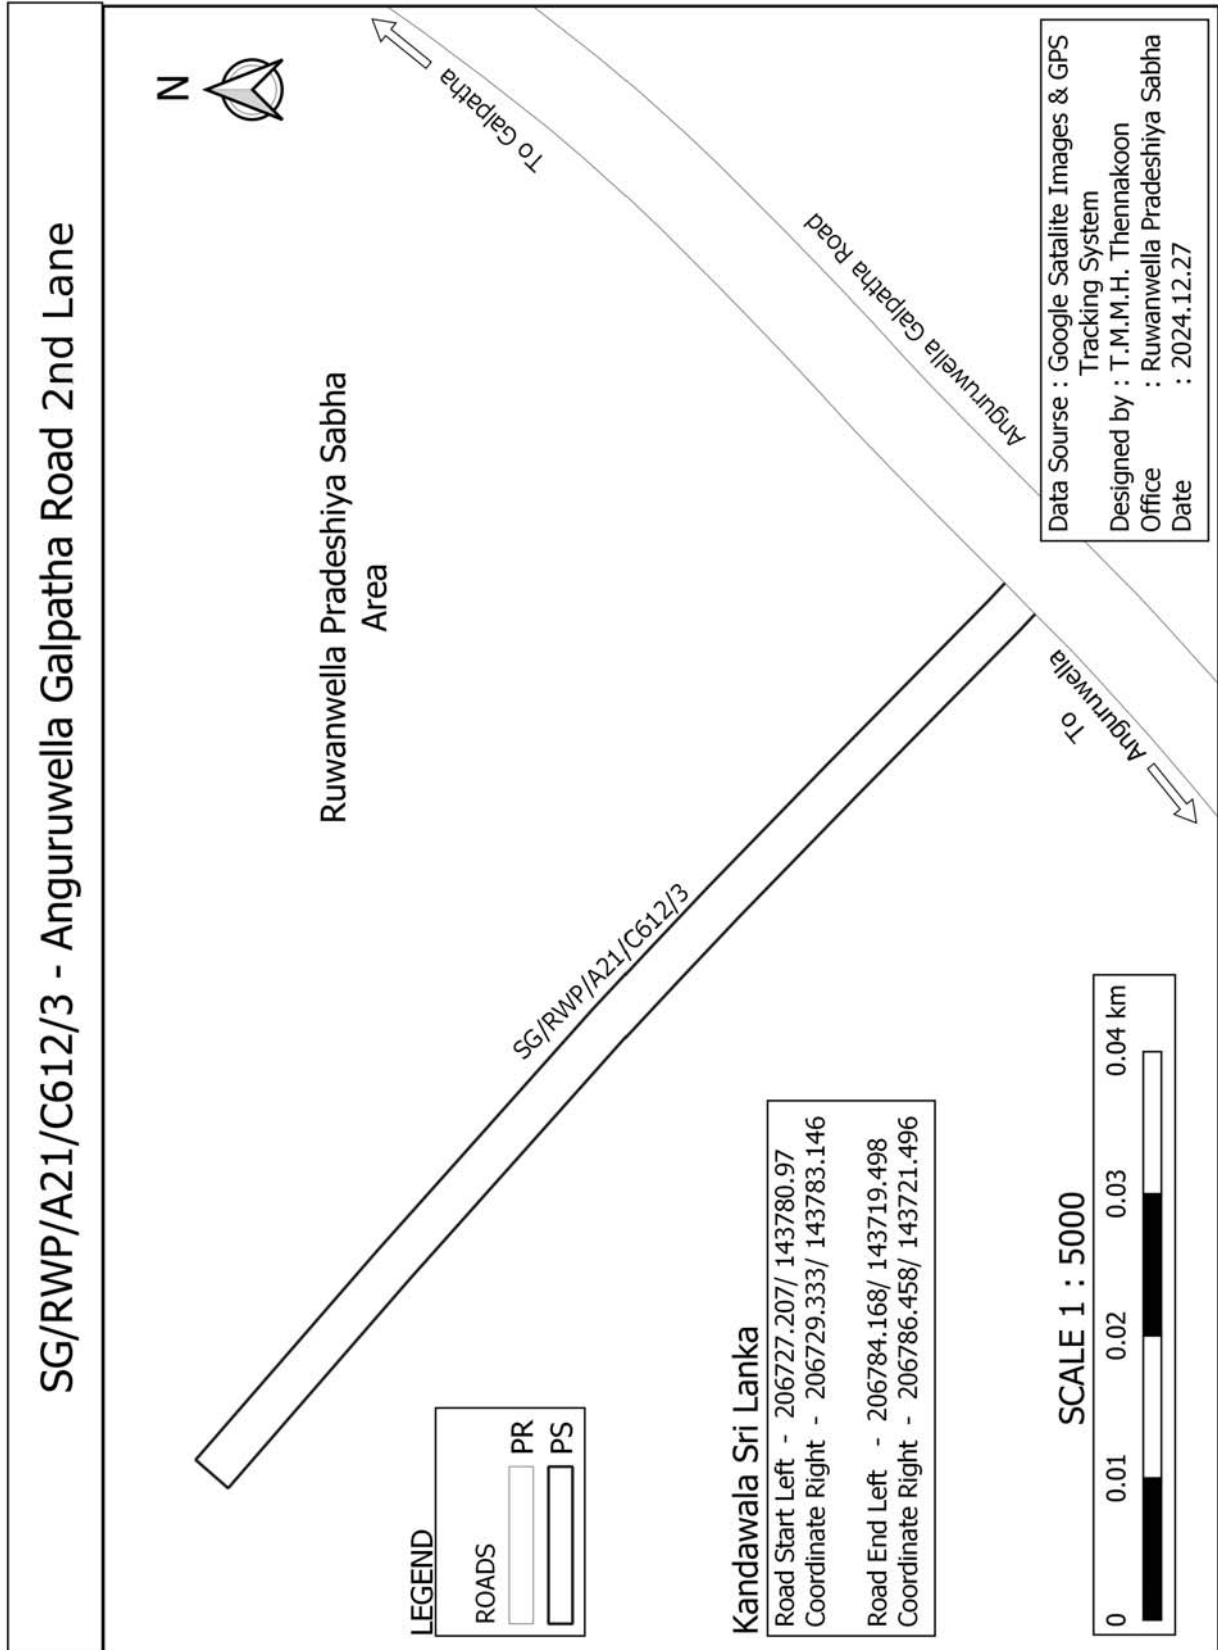


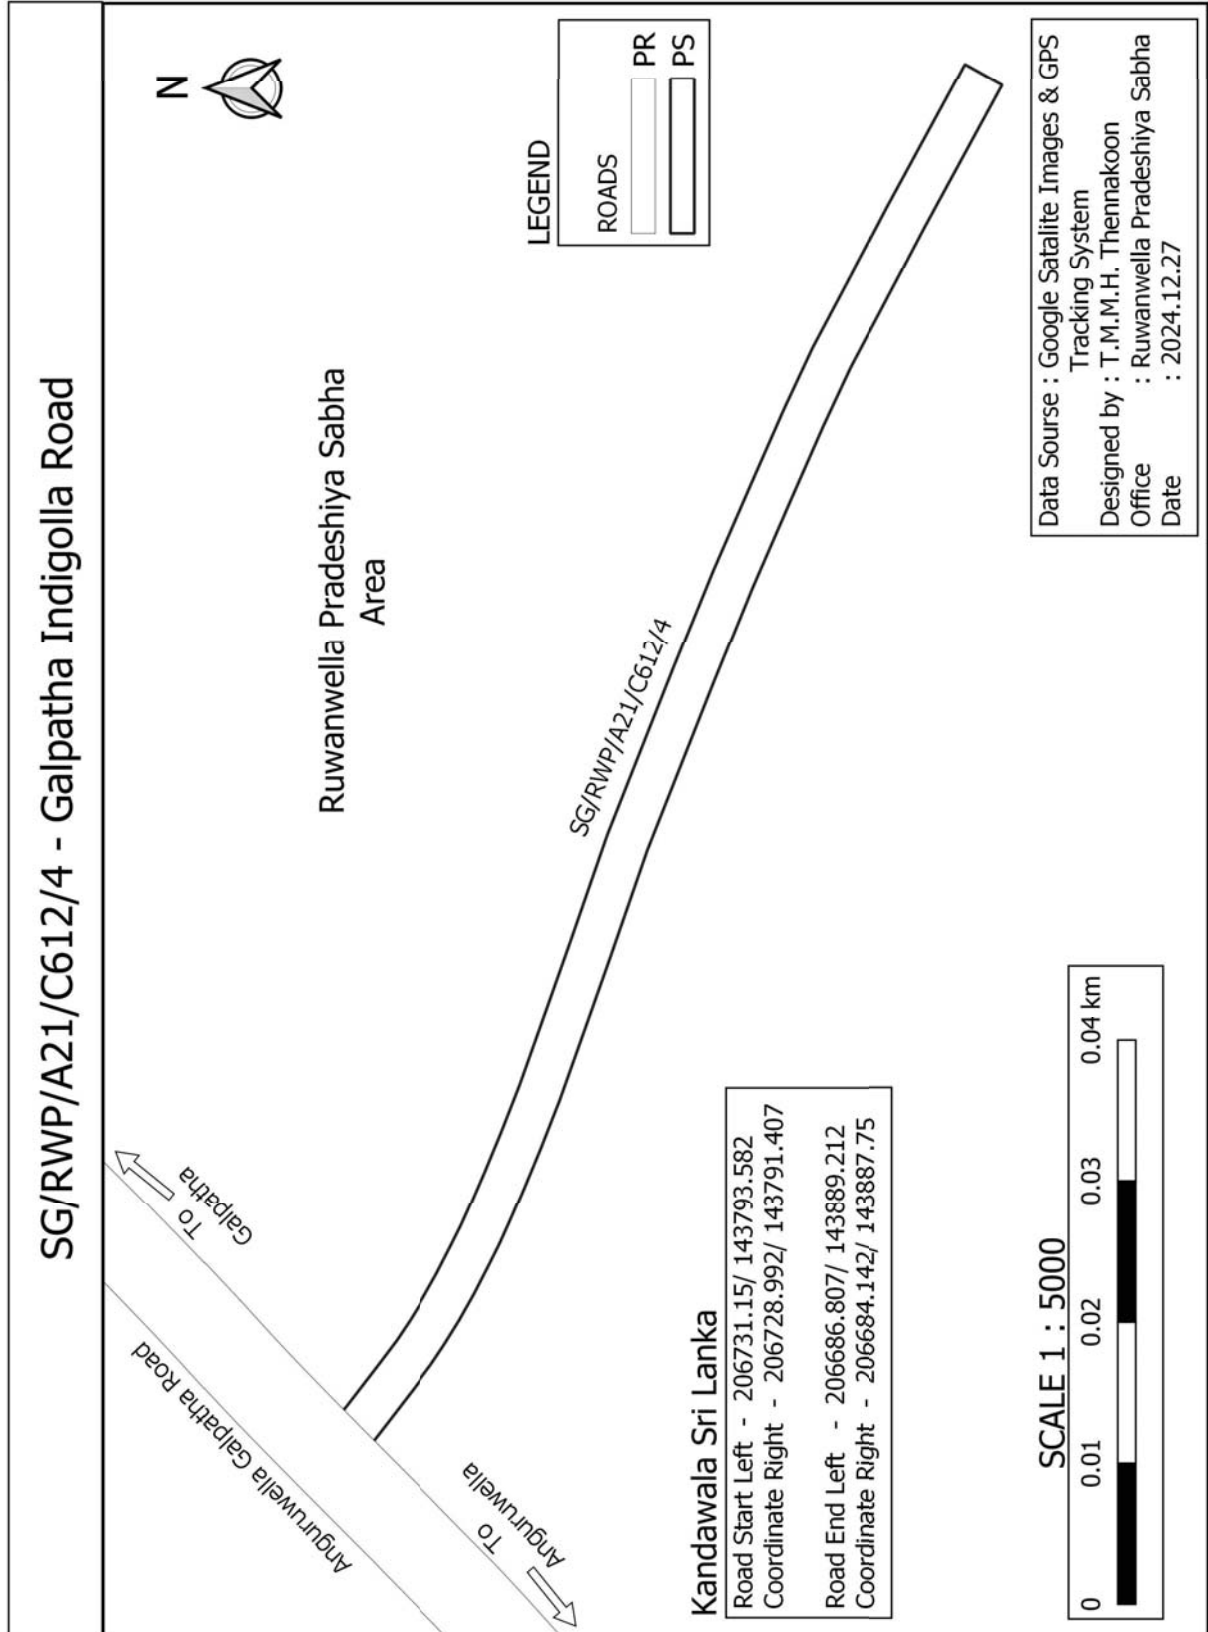


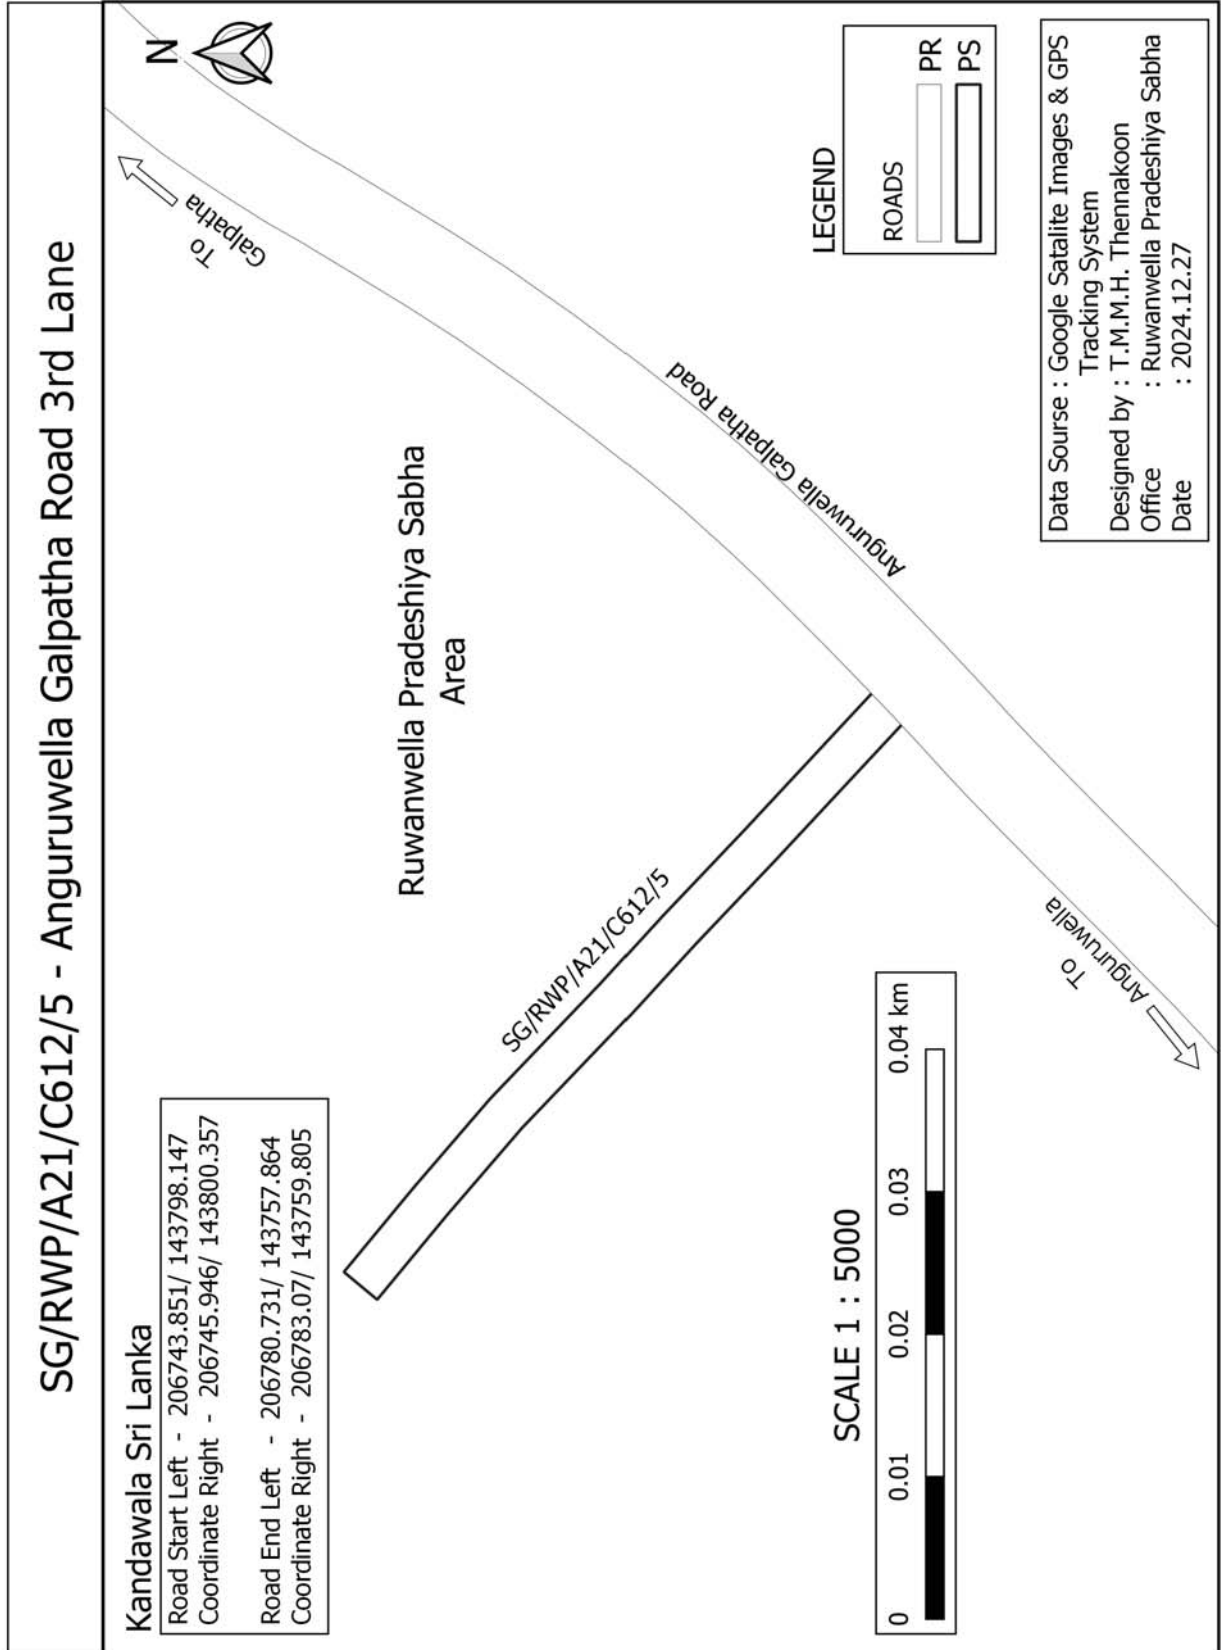


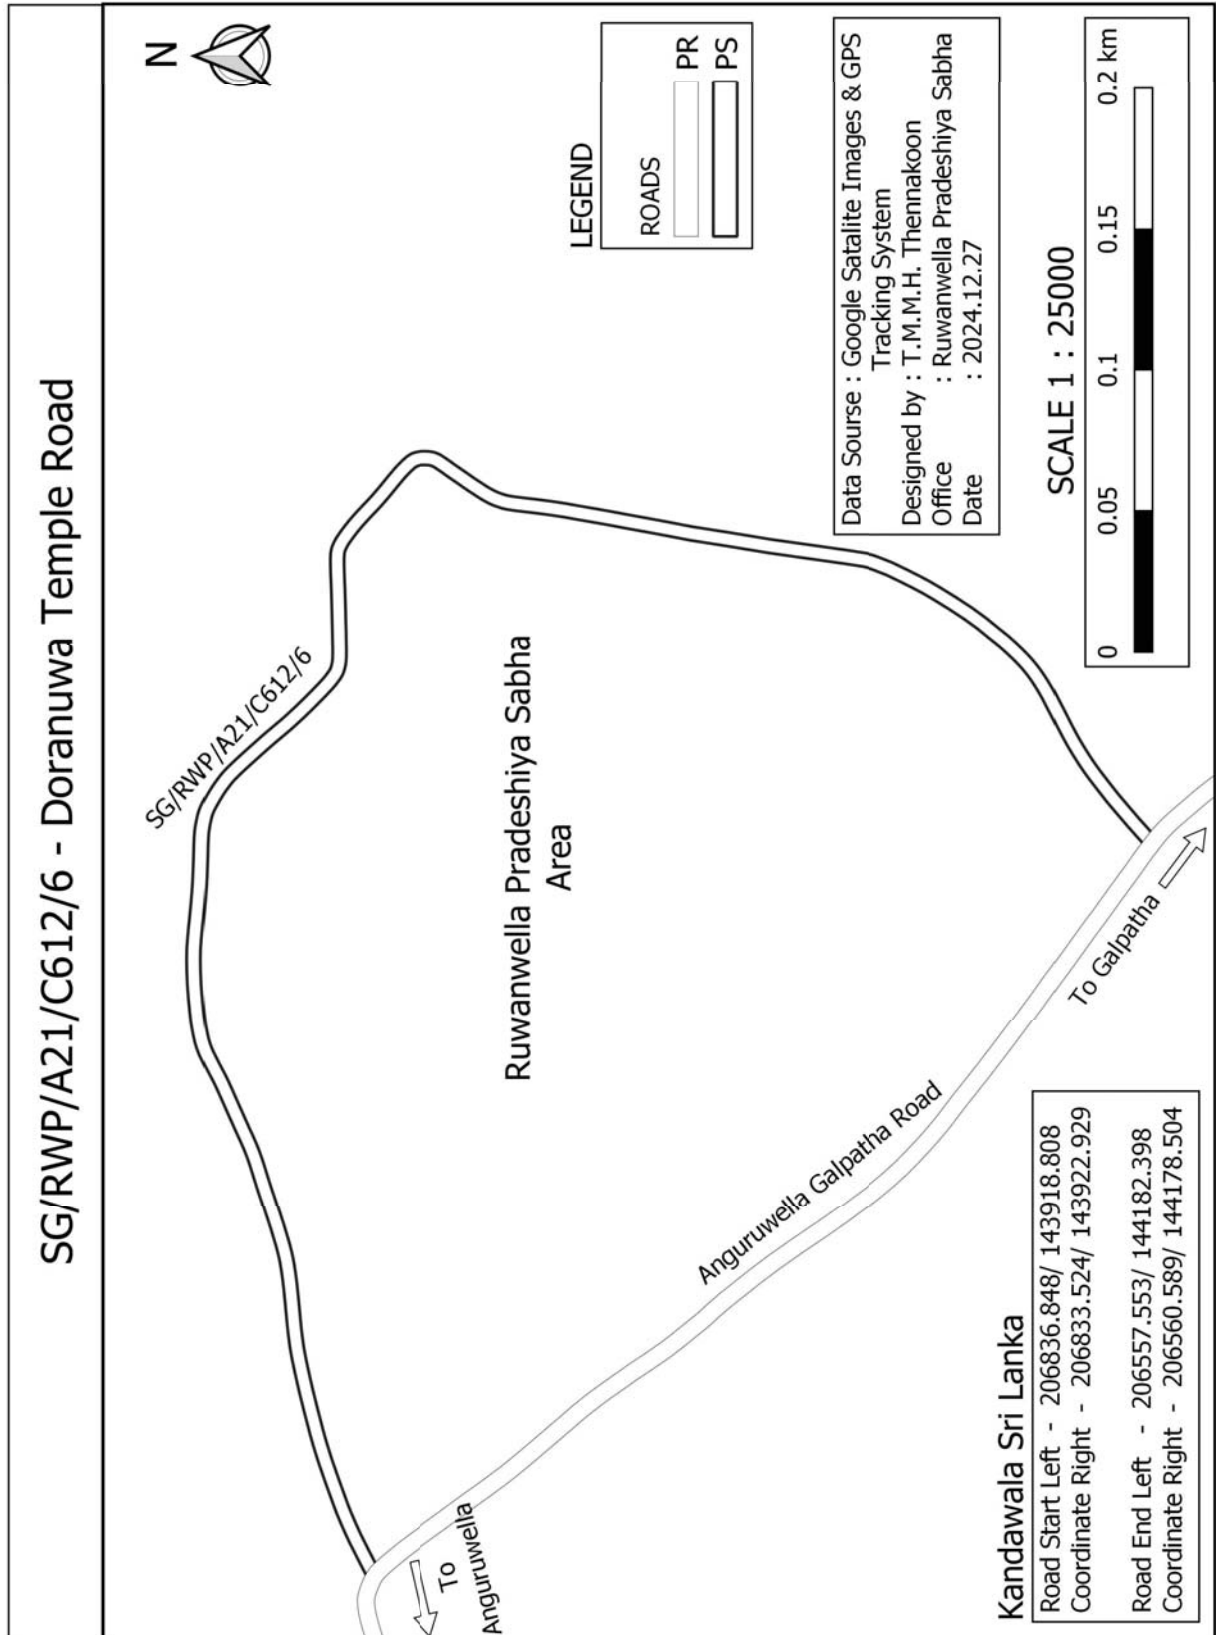


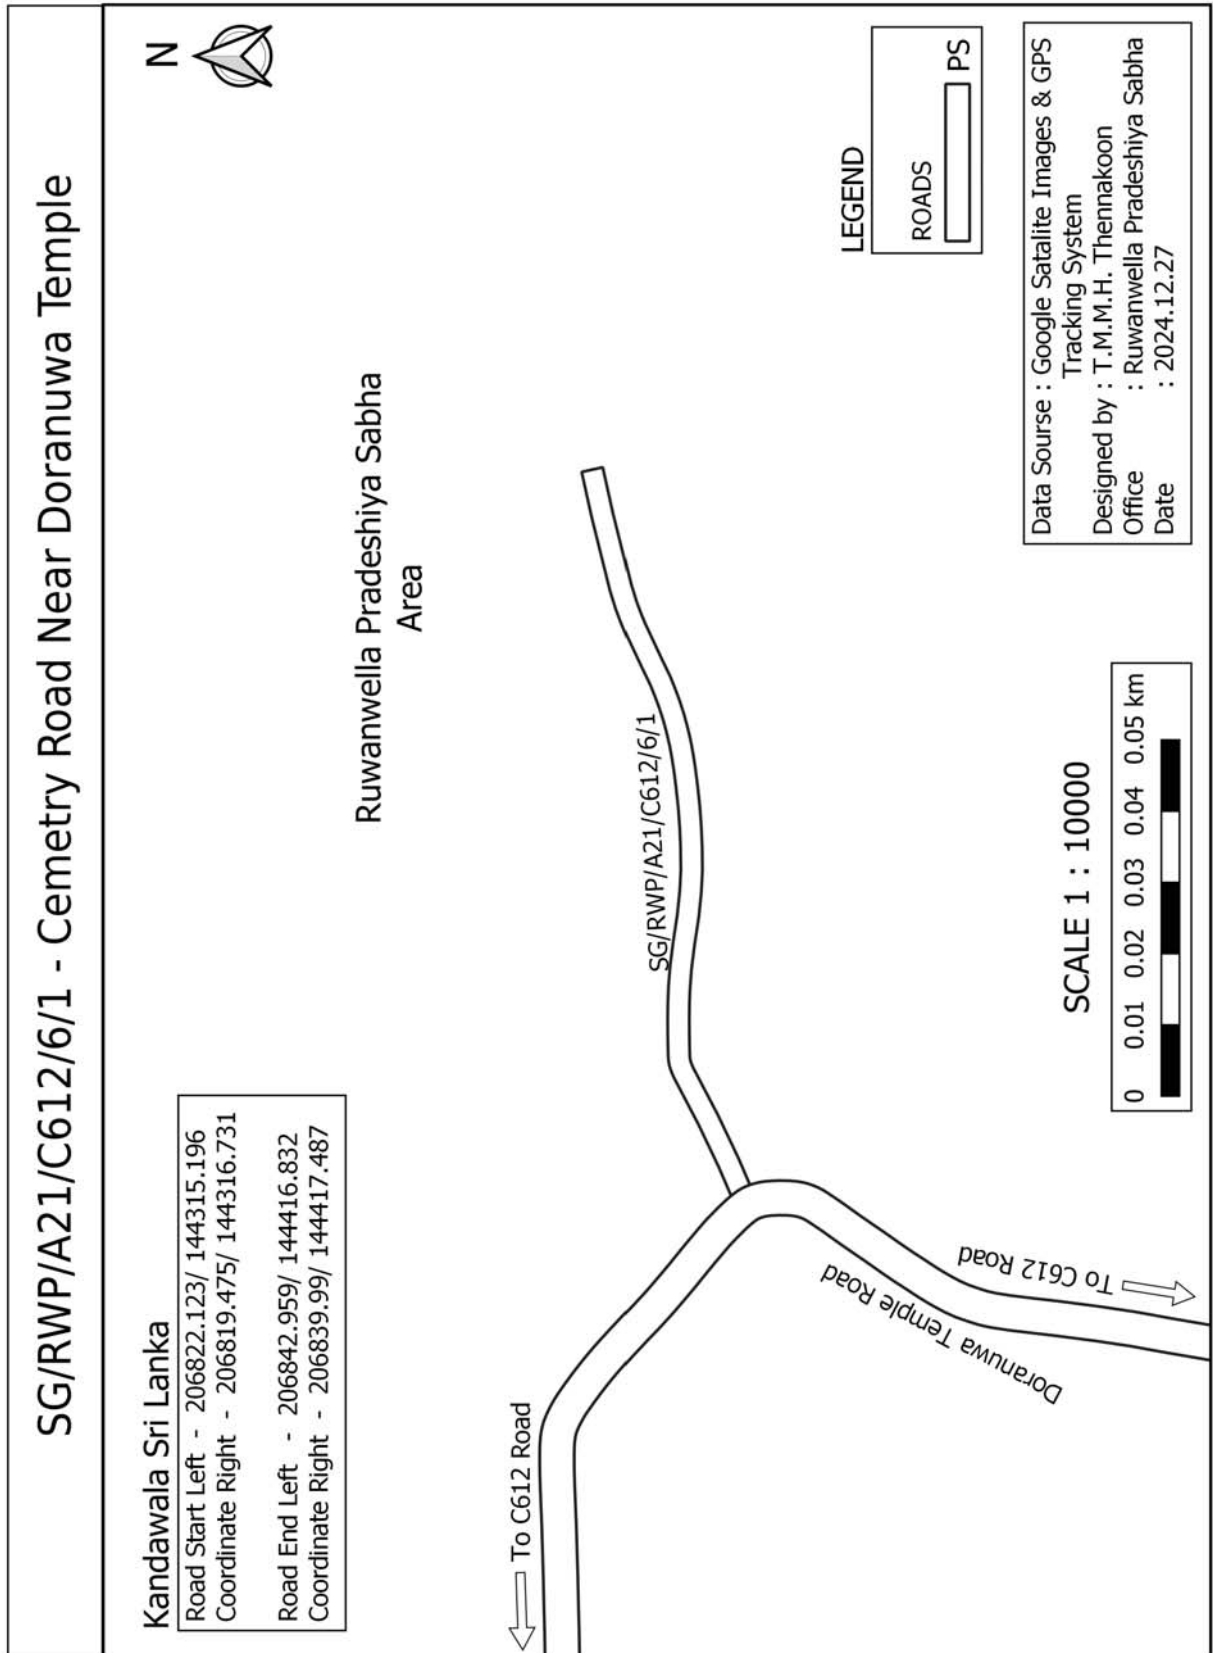


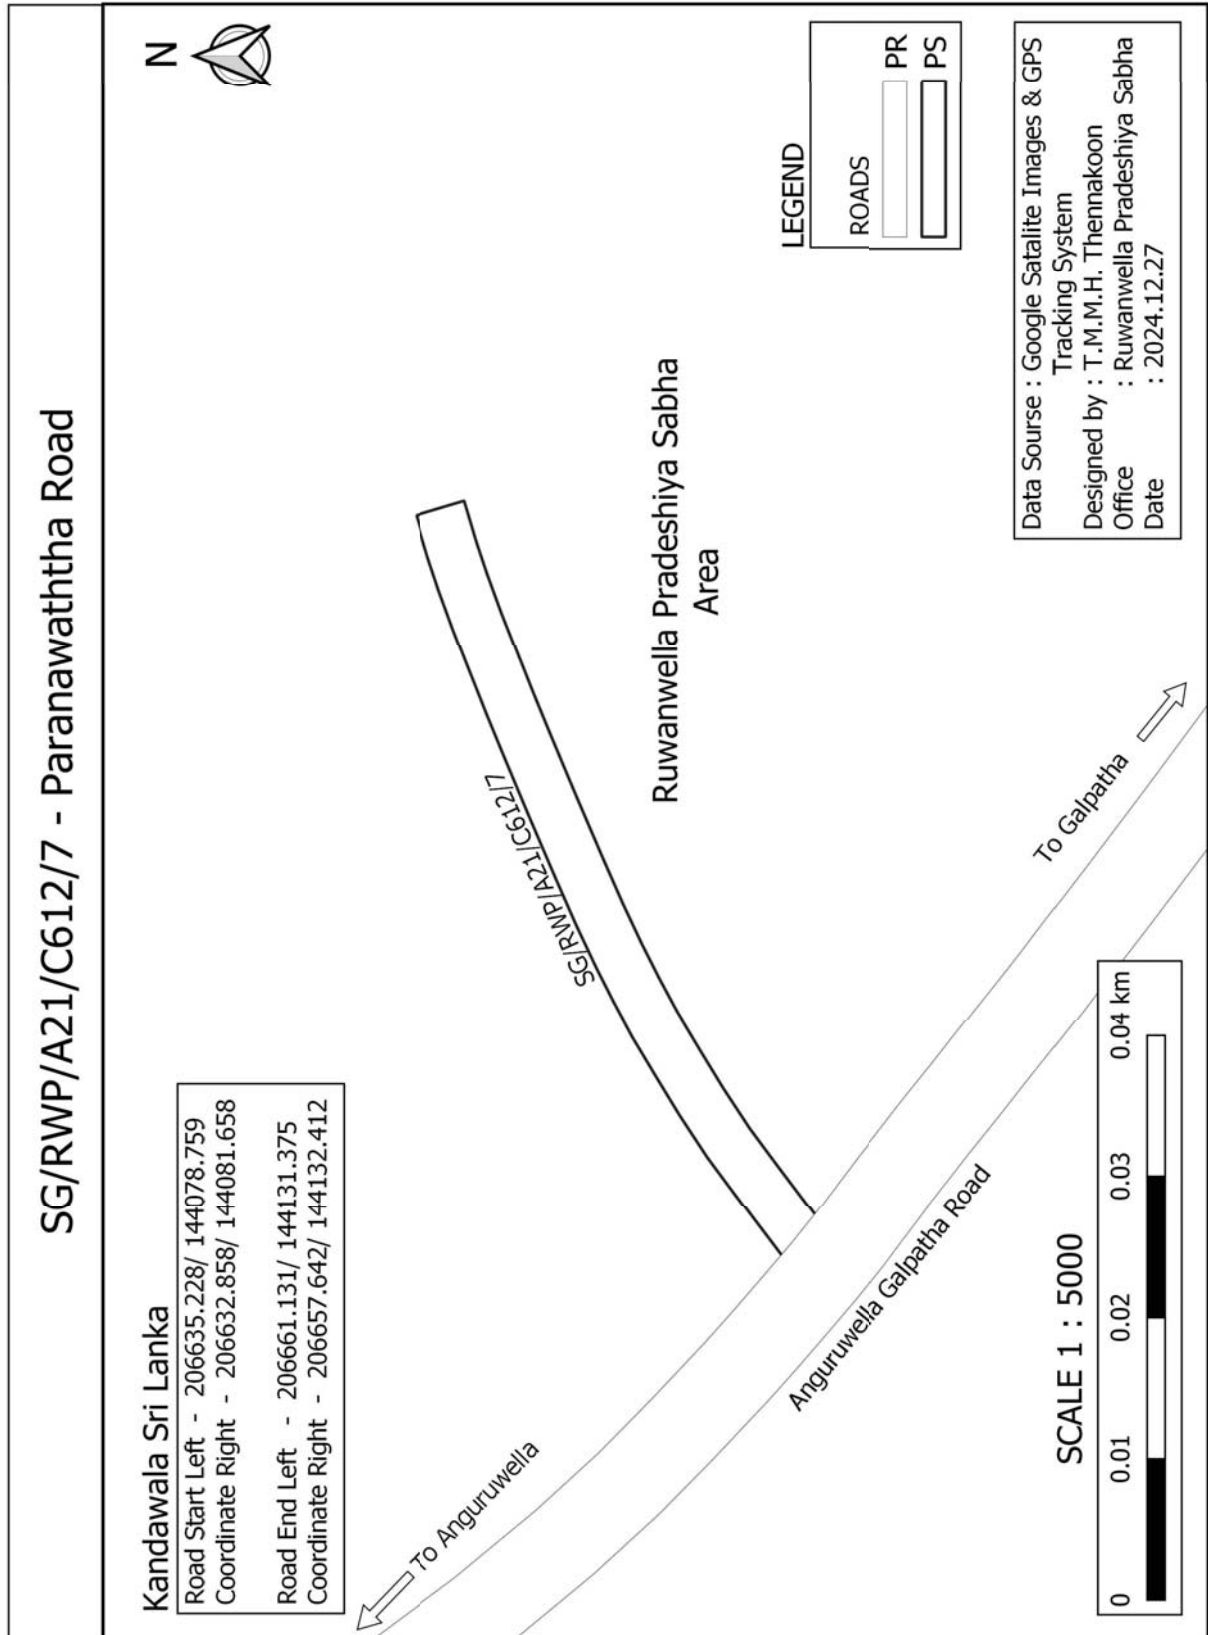


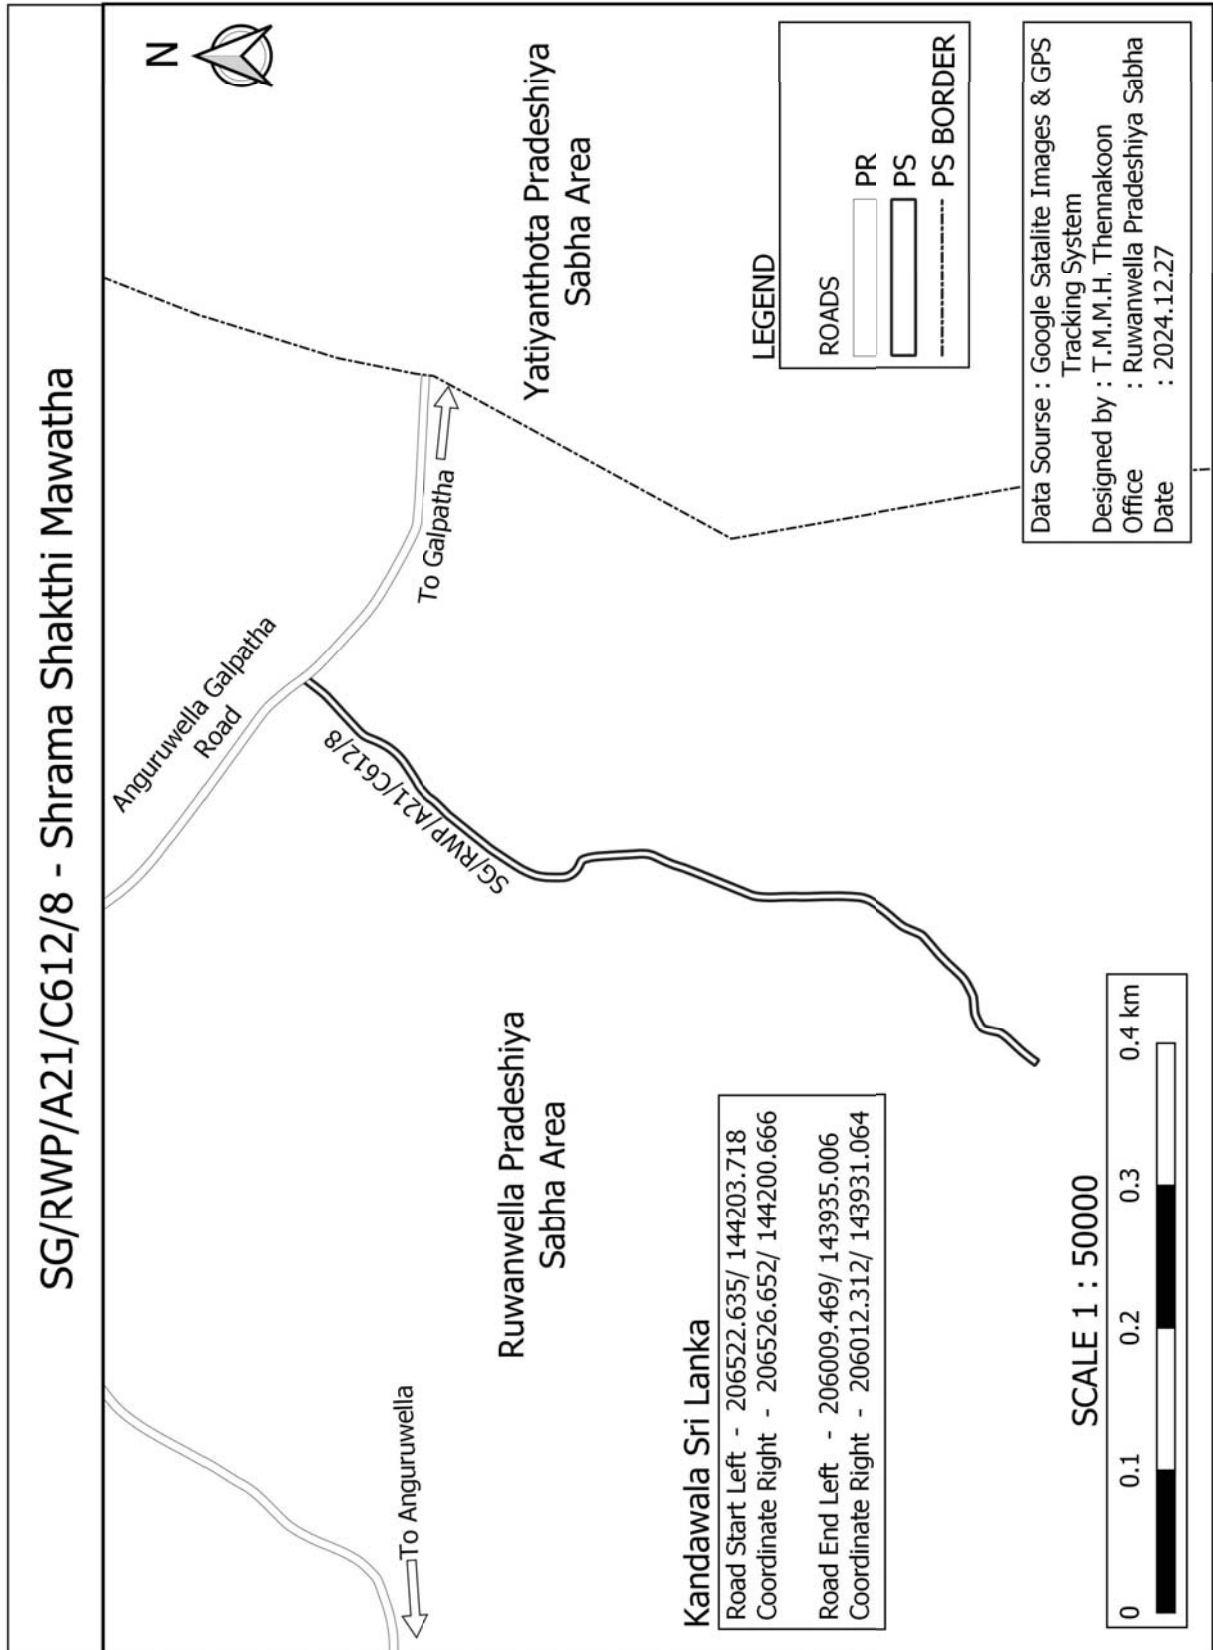


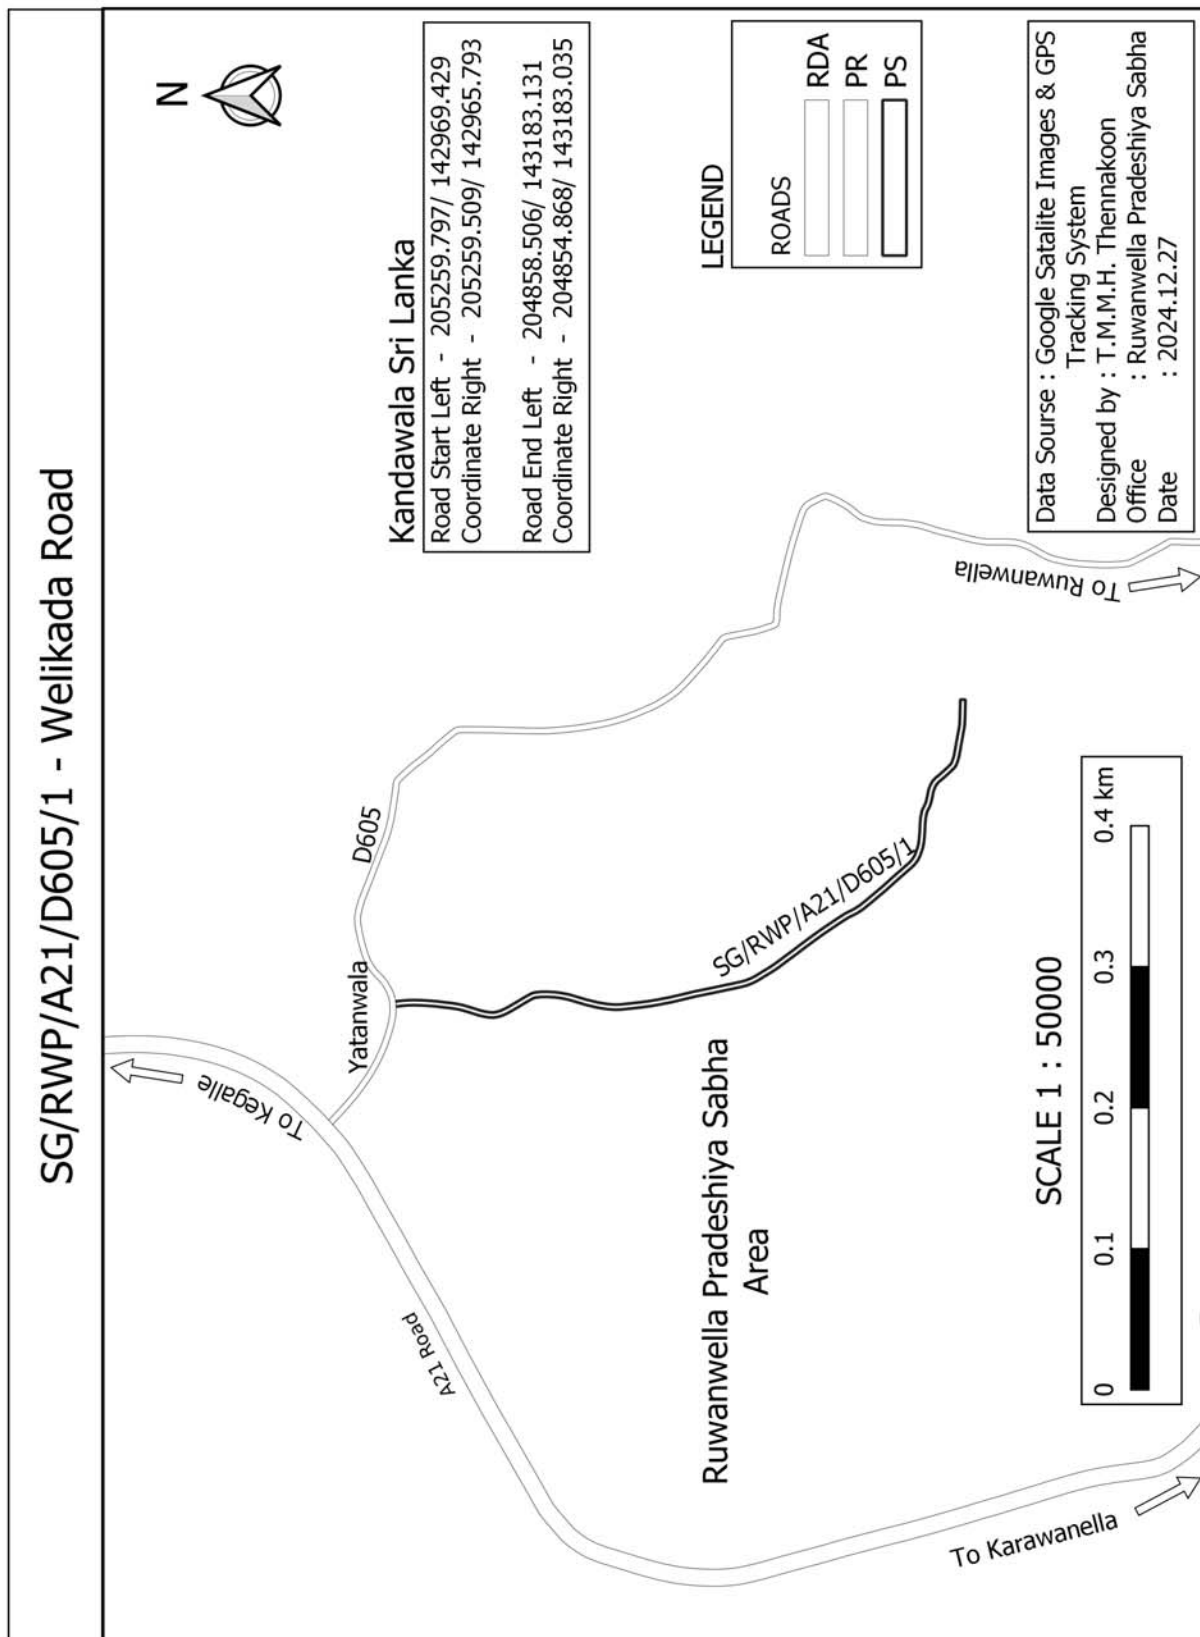


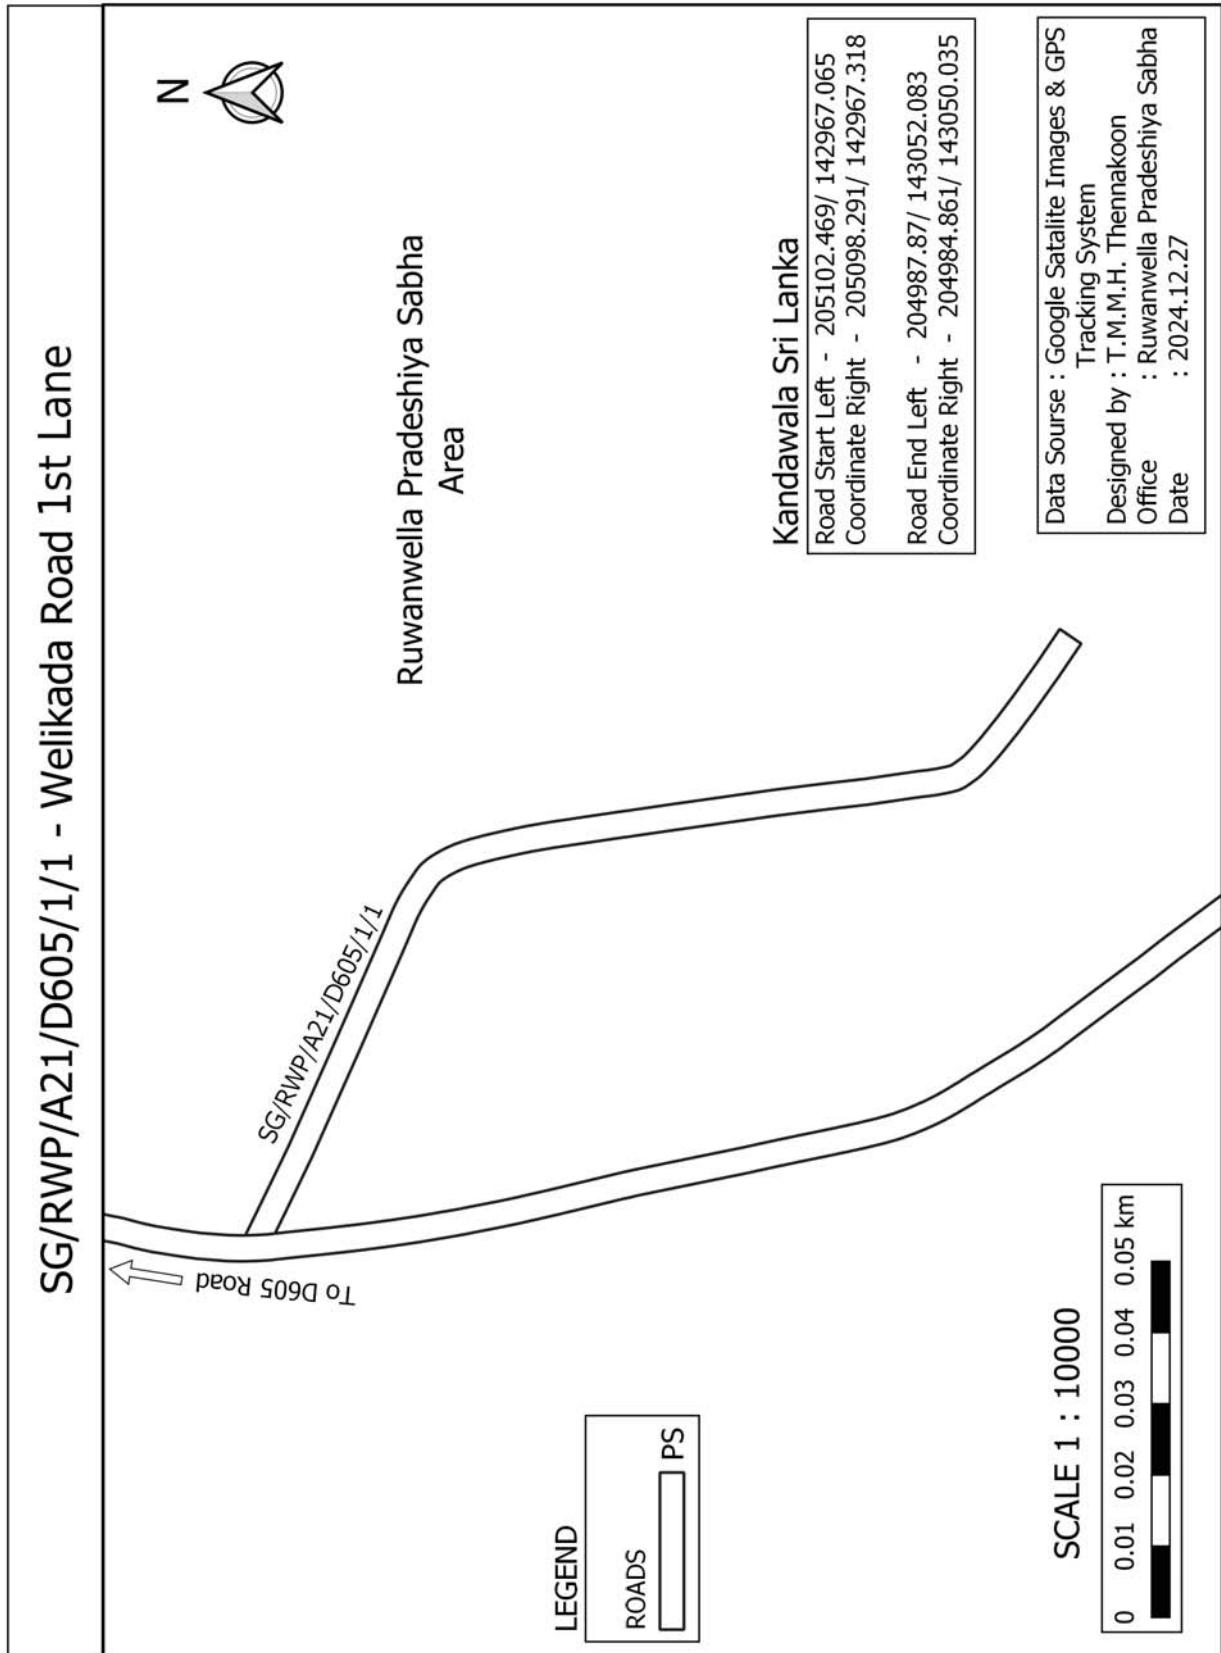


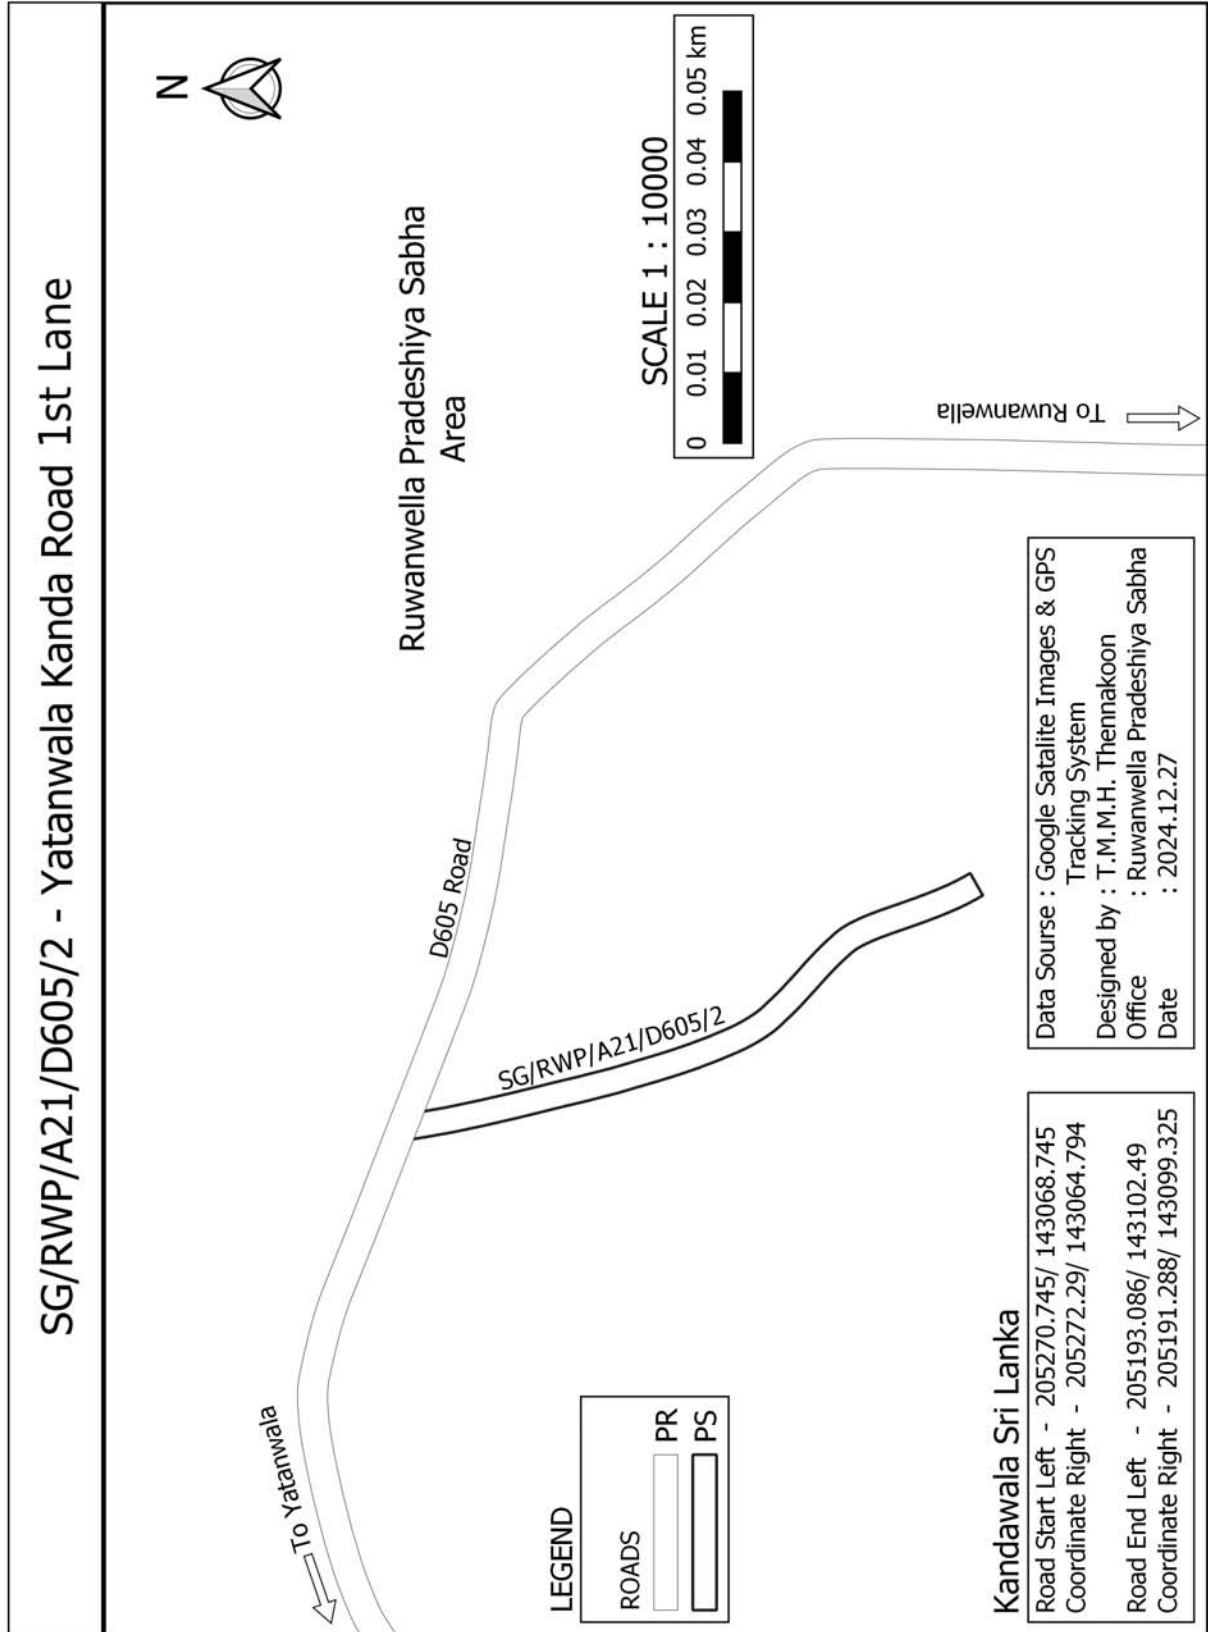

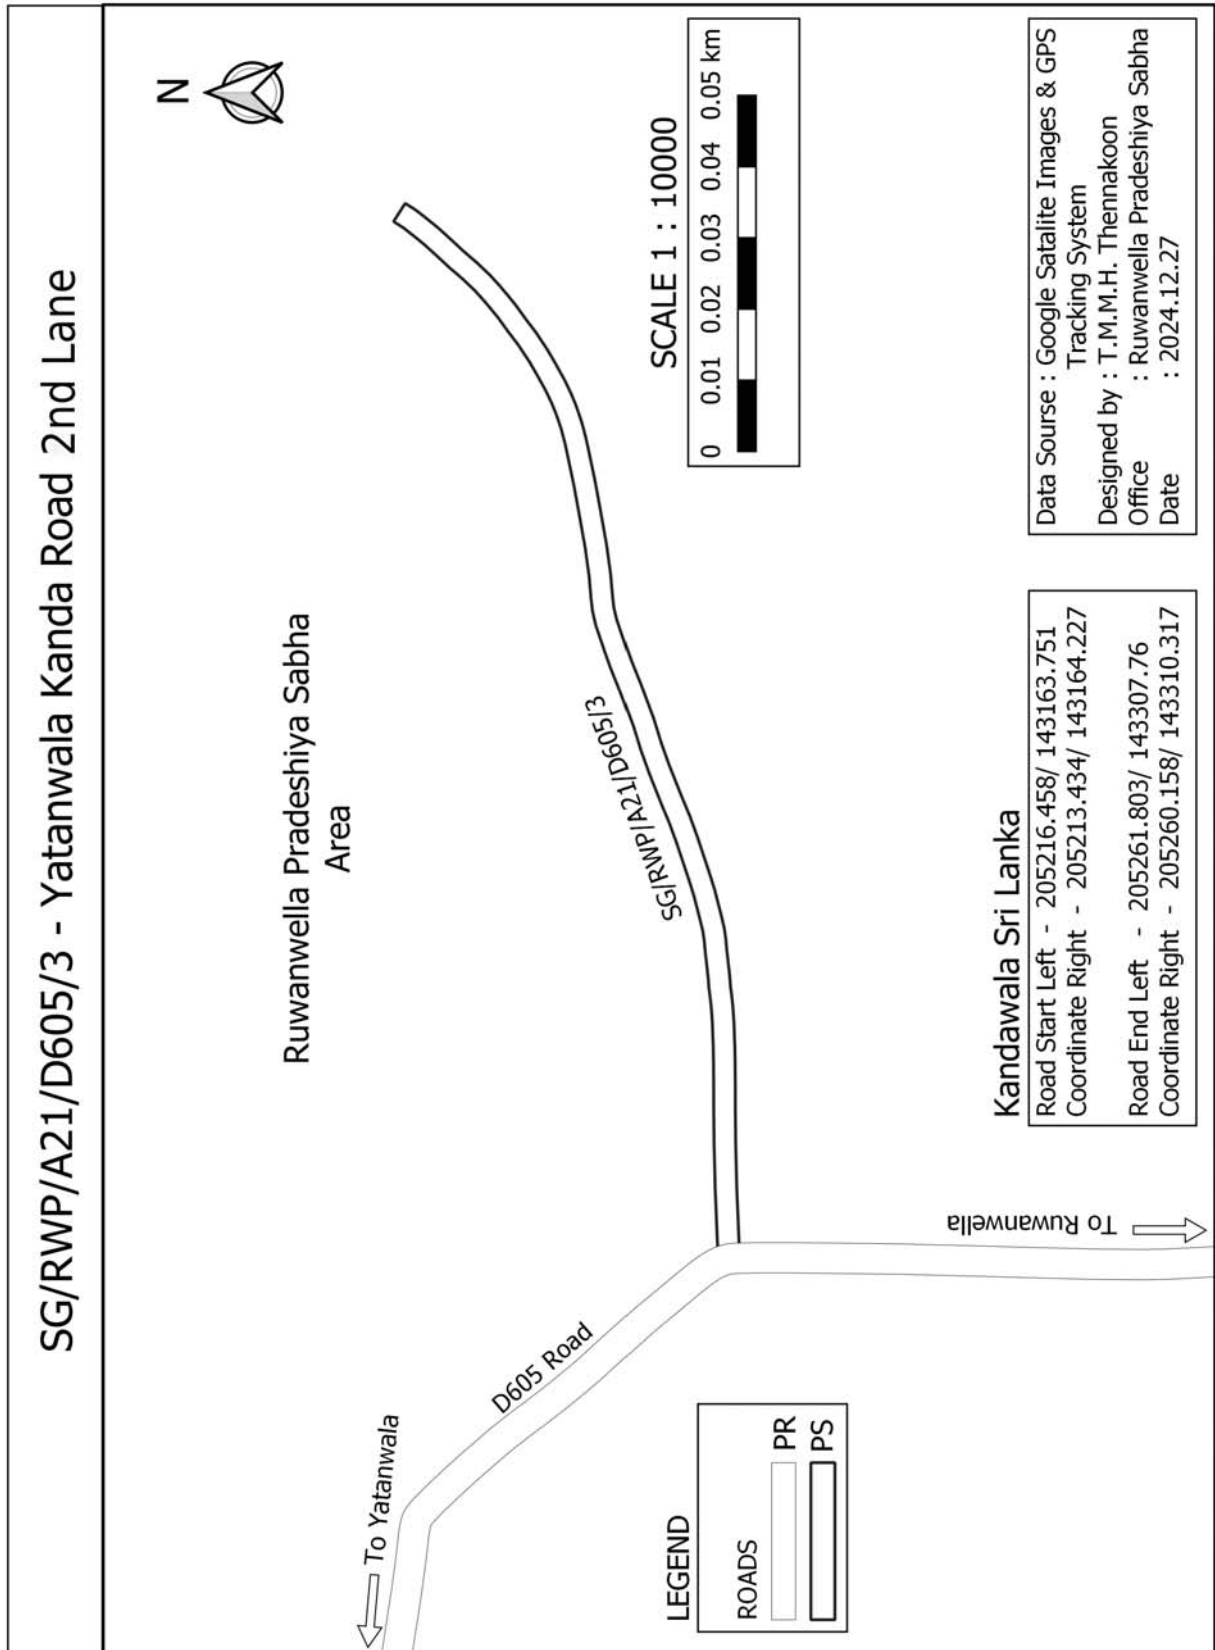

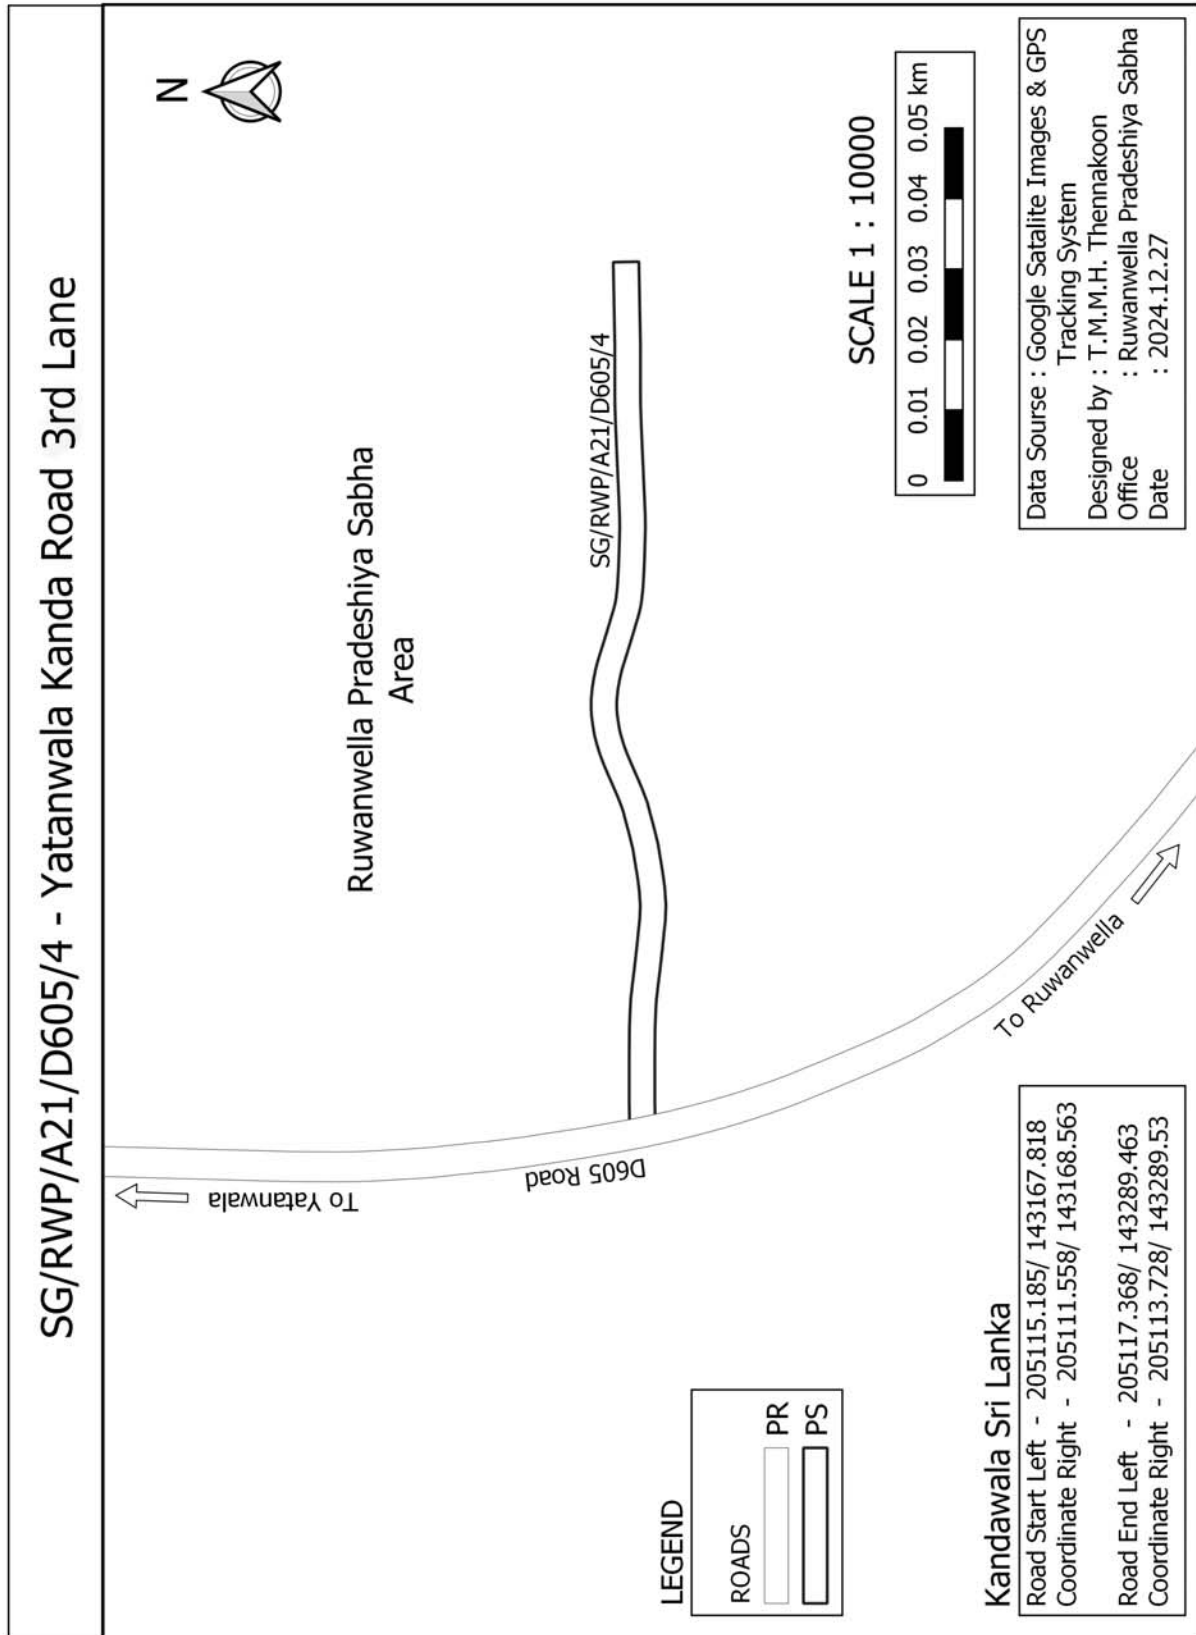

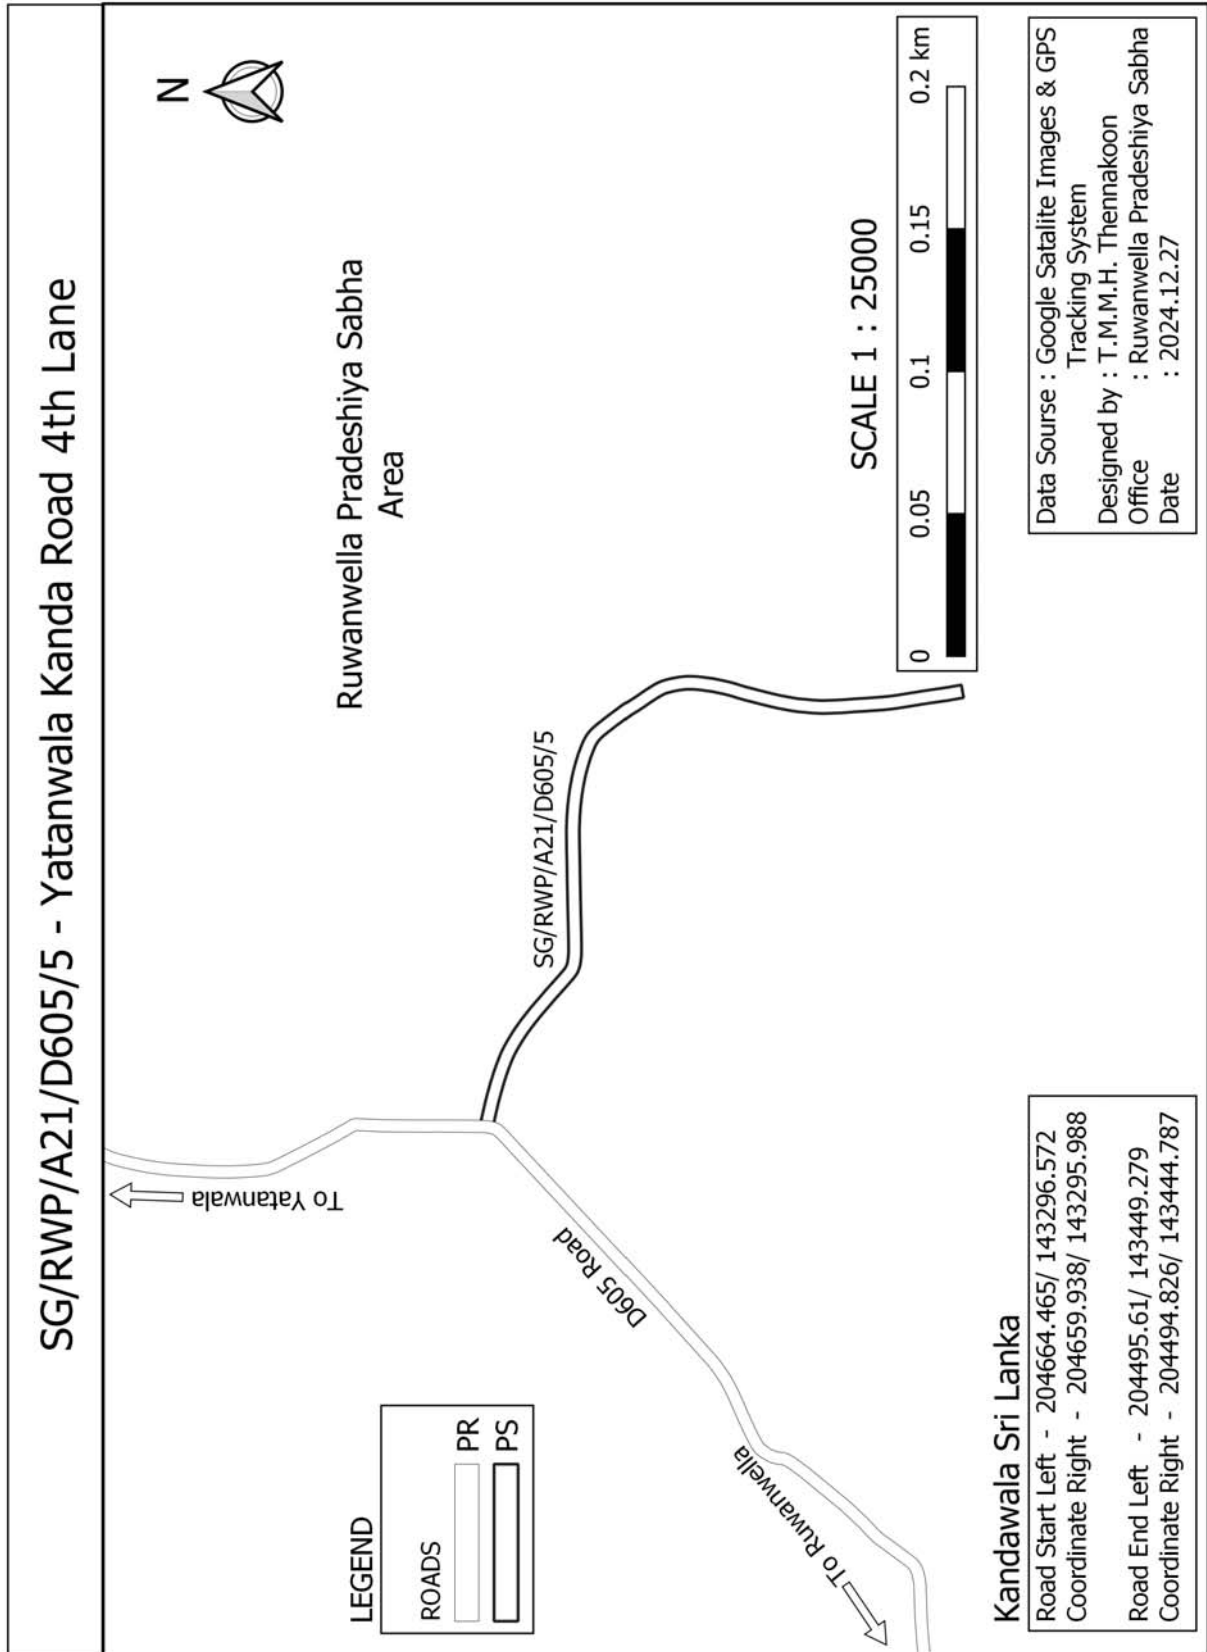

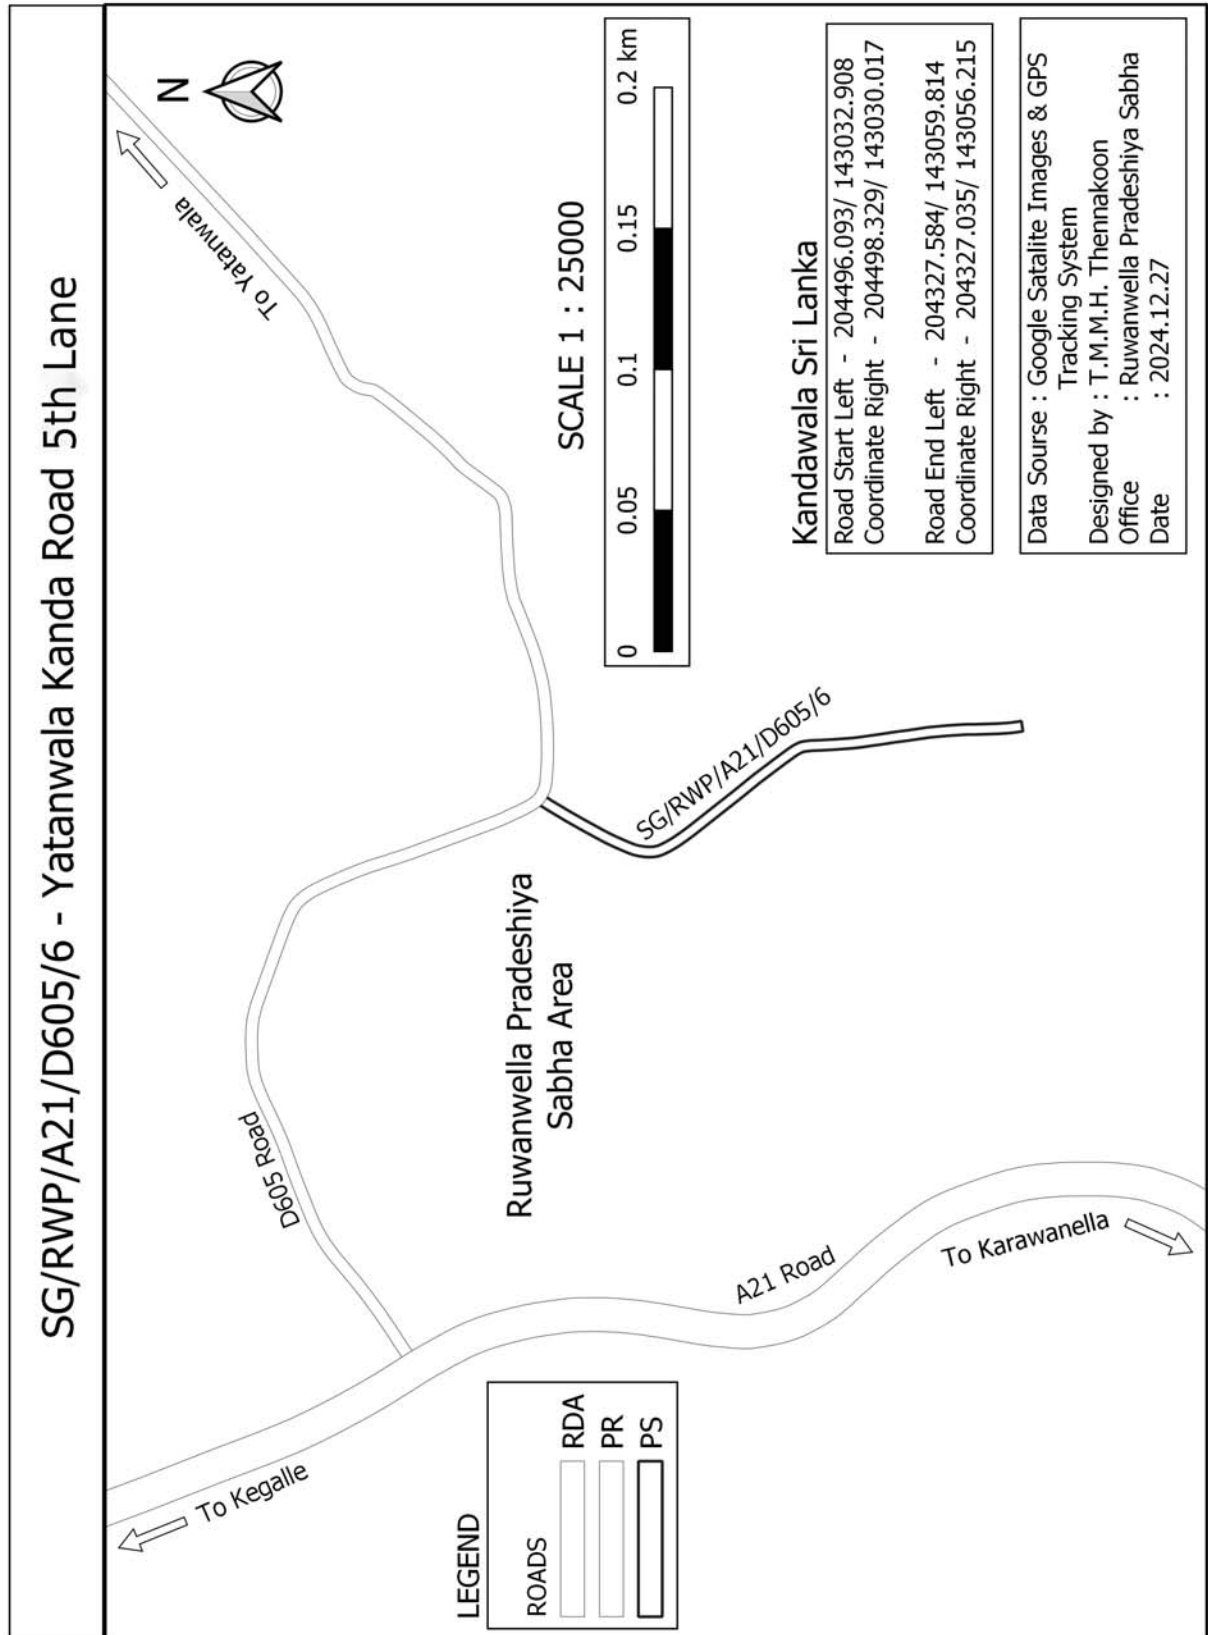

EOG 03-0192