



ශ්‍රී ලංකා ප්‍රජාතාන්ත්‍රික සමාජවාදී ජනරජයේ ගැසට් පත්‍රය

අති විශේෂ

අංක 2419/46 - 2025 ජනවාරි මස 18 වැනි සෙනසුරාදා - 2025.01.18

(රජයේ බලයපිට ප්‍රසිද්ධ කරන ලදී)

IV (ආ) වැනි කොටස - පළාත් සභා

පළාත් සභා නිවේදන

ගලිගමුව ප්‍රාදේශීය සභාව

1987 අංක 15 දරන ප්‍රාදේශීය සභා පනතේ 24 වන වගන්තිය සමඟ කියවිය යුතු, සබරගමුව පළාතේ ගරු ආණ්ඩුකාරතුමා විසින් අංක 2316/20 සහ 2023 ජනවාරි මස 24 වැනි දිනැති අති විශේෂ ගැසට් පත්‍රයේ ප්‍රකාශයට පත්කරනු ලැබ ඇති සබරගමුව පළාතේ ප්‍රාදේශීය සභා විසින් පවත්වාගෙන යනු ලබන පාරවල් හා පටු මාවත්වල සැලසුම් පිළියෙළ කිරීම හා නාම ලේඛනය දක්වමින් දැන්වීම් පළකිරීම පිළිබඳ නියෝග" මාලාවෙන් සබරගමුව පළාතේ ප්‍රාදේශීය සභාවලට පවරා දී ඇති කාර්යය අනුව, මෙහි පහත උපලේඛනයේ ඇතුළත් පාරවල් සහ පටු මාවත් ගලිගමුව ප්‍රාදේශීය සභාව සතු වී ඇති පාරවල් හා පටු මාවත් වශයෙන් ප්‍රකාශයට පත් කළ යුතු බව 2024.12.05 දින අංක 2024/12/05/50 ලේකම් තීරණ යටතේ තීරණය කරනු ලැබ ඇති බව මහජනතාවගේ දැනගැනීම සඳහා මෙයින් ප්‍රසිද්ධ කරනු ලැබේ.

එකී උපලේඛනයේ ඇතුළත් යම් පාරක් හෝ පටු මාවතක් කිසියම් ඉඩමක් හරහා හෝ යම් ඉඩමක කොටසකට ඇතුළත් වන බව, ඒ ඉඩමට හිමිකම් කියනු ලබන පාර්ශවයේ මතය වේ නම්, එකී ඉඩමට තමන්ගේ ඇති අයිතිය ඔප්පු කිරීම සඳහා මෙම නිවේදනයේ දින සිට මාස තුනක කාලයක් ඉකුත්වීමට පෙර නිසි අධිකරණයේ නඩුවක් පැවරීමට ක්‍රියා කළ යුතු බවත් මෙයින් නිවේදනය කරනු ලැබේ. තව දුරටත් එසේම, එකී මාස තුනක කාලය අවසන් වීමට පෙර එවැනි නඩුවක් පවරා නැති එකී උපලේඛනයේ ඇතුළත් සෑම පාරක් ම සහ පටු මාවතක් ම ගලිගමුව ප්‍රාදේශීය සභාව සතු කරනු ලැබ ඇති පාරක් හෝ පටු මාවතක් ලෙස සලකනු ලබන බව වැඩිදුරටත් නිවේදනය කරනු ලැබේ.

නවෝදා ක්‍රිශාන්ති,
ලේකම් හා බලතල, කාර්ය කර්තව්‍ය
ක්‍රියාත්මක කිරීමේ නිලධාරී,
ගලිගමුව ප්‍රාදේශීය සභාව.

2025 ජනවාරි 07 වැනි දින,
ගලිගමුව ප්‍රාදේශීය සභාව,
පිටගල්දෙණිය දී ය.



තුන්වන උපලේඛනය

08 වන වගන්තිය

අනු අංකය.	පාරේච්ඡි කේතය	පාරේ නම	ආරම්භක බාණ්ඩංක (කළුවල ශ්‍රී ලංකා)		අවසාන බාණ්ඩංක (කළුවල ශ්‍රී ලංකා)		පාරේ දිග (මීටර්)	පාරේ සාමාන්‍ය පළල (මීටර්)	සංවර්ධිත පළල (මීටර්)
			වම	දකුණ	වම	දකුණ			
1	SG/GLP/ A01/ 01	කඩිකුඹුර මාර්ගය	226029.675/ 149379.343	226025.869/ 149379.393	226072.921/ 149453.844	226070.583/ 149456.659	100.4	3.66	2.44
2	SG/GLP/ A01/ 01/ 01	කඩිකුඹුර පළමු පටුමග	226031.784/ 149421.043	226030.689/ 149416.722	226004.948/ 149440.356	226008.765/ 149438.556	166.98	4	3.66
3	SG/GLP/ A01/ 01/ 02	කඩිකුඹුර දෙවන වන පටුමග	226043.012/ 149435.981	226040.742/ 149433.725	226014.537/ 149506.707	226013.131/ 149503.832	84.64	3.2	2.44
4	SG/GLP/ A01/ 02	හින්දු පාසල් මාර්ගය	225937.106/ 149314.764	225934.72/ 149312.341	225881.048/ 149351.682	225878.032/ 149350.112	78.92	3.4	2.2
5	SG/GLP/ A01/ 02/ 01	හින්දු පාසල පළමු පටුමග	225883.013/ 149339.294	225884.342/ 149337.634	225853.175/ 149281.586	225854.111/ 149279.818	70.88	2	2
6	SG/GLP/ A01/ 03	නැව්ගල පන්සල මාර්ගය	225929.263/ 149129.13	225929.958/ 149132.144	226285.238/ 149109.837	226284.247/ 149112.731	487.78	3.04	2.44
7	SG/GLP/ A01/ 03/ 01	විහාරභේන පළමු පටුමග	226033.609/ 149092.507	226035.779/ 149090.236	226066.742/ 148911.468	226069.42/ 148912.907	212.36	3.04	2.44

අනු අංකය	පාරම්පරික කේතය	පාර්ශ්ව නම	ආරම්භක බණ්ඩාංක (කදවල ශ්‍රී ලංකා)		අවසාන බණ්ඩාංක (කදවල ශ්‍රී ලංකා)		පාරේ දිග (මීටර්)	පාරේ සාමාන්‍ය පළල (මීටර්)	සංවර්ධිත පළල (මීටර්)
			වම	දකුණ	වම	දකුණ			
8	SG/ GLP/ A01/ 03/ 02	නැව්ගල නො 2 වත්ත මාර්ගය	226114.566/ 149144.241	226112.073/ 149141.701	226843.083/ 149172.977	226843.469/ 149175.992	822.46	3.04	2.44
9	SG/ GLP/ A01/ 03/ 03	නැව්ගල පළමු පටුමග	226218.651/ 149085.125	226221.709/ 149084.985	226277.538/ 149023.704	226274.749/ 149024.914	171.43	3.04	2.44
10	SG/ GLP/ A01/ 03/ 04	නැව්ගල දෙවන පටුමග	226281.621/ 149109.05	226285.238/ 149109.837	226303.532/ 149062.951	226306.82/ 149064.56	52.13	3.66	2.6
11	SG/ GLP/ A01/ 04	මහවෙල මාර්ගය	225875.773/ 149058.894	225875.133/ 149055.921	225710.968/ 149093.763	225712.567/ 149091.179	187.57	3.04	2.44
12	SG/ GLP/ A01/ 04/ 01	මහවෙල පළමු පටුමග	225742.236/ 149095.418	225738.726/ 149096.498	225717.729/ 149175.167	225714.083/ 149175.498	101.3	3.66	2.44
13	SG/ GLP/ A01/ 05	විහාරභේන මාර්ගය	225890.515/ 148971.397	225889.861/ 148974.366	226017.852/ 149024.843	226017.272/ 149027.851	153.38	3.04	2.44
14	SG/ GLP/ A01/ 06	බිසෝවෙල එහොඳවත්ත මාර්ගය	225892.783/ 148932.203	225894.463/ 148928.951	225541.745/ 149070.98	225538.221/ 149069.992	523.15	3.66	2.44

අනු අංකය.	පාරේච්ඡි කේතය	පාරේ නම	ආරම්භක බණ්ඩාංක (කළුවල ලංකා)		අවසාන බණ්ඩාංක (කළුවල ශ්‍රී ලංකා)		පාරේ දිග (මීටර්)	පාරේ සාමාන්‍ය පළල (මීටර්)	සංවර්ධිත පළල (මීටර්)
			වම	දකුණ	වම	දකුණ			
15	SG/GLP/A01/06/01	බිසෝවෙල එහොඩ්වත්ත පළමු වන පවුම	225692.403/ 148923.473	225698.715/ 148925.947	225425.777/ 148908.071	225428.493/ 148904.768	281.71	4.26	2.44
16	SG/GLP/A01/07	නැව්ගල විහාර වත්ත මාර්ගය	225925.752/ 148893.638	225924.473/ 148896.428	225968.399/ 148945.159	225965.923/ 148943.396	81.85	3.04	2.44
17	SG/GLP/A01/08	රණවිරු සූරියබණ්ඩාර මාර්ගය	225967.459/ 148798.084	225966.321/ 148800.942	226171.504/ 148744.269	226172.379/ 148747.181	267.68	3.04	2.44
18	SG/GLP/A01/09	වරකාපිටිය මාර්ගය	226027.71/ 148647.384	226026.862/ 148650.952	227061.335/ 148459.783	227063.93/ 148463.084	1169.5	3.66	2.44
19	SG/GLP/A01/09/01	ගලිගමුව පල්ලේගම නැව්ගල මාර්ගය	226149.443/ 148632.179	226147.54/ 148634.549	226762.083/ 149181.296	226765.735/ 149181.514	2464.36	3.04	2.44
20	SG/GLP/A01/09/01/01	පල්ලේගම ගමමැද මාර්ගය	226446.291/ 148700.374	226448.7/ 148702.333	226536.423/ 148652.686	226539.393/ 148653.335	119.23	3.04	3.04

අනු අංකය	පාරම්පරික කේතය	පාරේ නම	ආරම්භක බණ්ඩාංක (කළමනාකරණ ලංකා)		අවසාන බණ්ඩාංක (කළමනාකරණ ලංකා)		පාරේ දිග (මීටර්)	පාරේ සාමාන්‍ය පළල (මීටර්)	සංවර්ධිත පළල (මීටර්)
			වම	දකුණ	වම	දකුණ			
21	SG/ GLP/ A01/ 09/ 01/ 02	පිල්ල ලගව යන මාර්ගය	226456.595/ 148778.692	226453.643/ 148777.956	226335.417/ 148934.365	226333.133/ 148932.358	234.78	3.04	2.44
22	SG/ GLP/ A01/ 09/ 01/ 02/ 01	කන්දේවත්ත මාර්ගය	226358.521/ 148893.613	226357.962/ 148895.988	226469.863/ 148905.064	226470.698/ 148907.356	119.69	2.44	2.44
23	SG/ GLP/ A01/ 09/ 02	වරකාපිටිය පළමු පටුම	226810.628/ 148527.592	226813.674/ 148527.151	226935.027/ 148467.496	226937.376/ 148469.425	155.66	3.04	2.44
24	SG/ GLP/ A01/ 10	ගලිගමුව පාසල් මාර්ගය	226021.847/ 148509.569	226021.764/ 148506.368	225905.916/ 148424.212	225907.207/ 148421.284	196.56	3.2	2.44
25	SG/ GLP/ A01/ 11	පල්ලියවත්ත කනත්ත මාර්ගය	226060.125/ 148325.478	226059.375/ 148328.478	226283.166/ 148274.216	226285.818/ 148275.701	273.26	3.04	2.44
26	SG/ GLP/ A01/ 12	බල්ලපාන බිසෝවෙල මාර්ගය	226120.646/ 148102.29	226121.246/ 148099.305	225539.947/ 148368.027	225537.455/ 148366.287	704.26	3.04	3.04
27	SG/ GLP/ A01/ 12/ 01	ආදානාගාර මාර්ගය පළමු පටුම	225793.088/ 148256.137	225786.712/ 148256.431	225781.821/ 148386.576	225780.618/ 148383.612	171.66	3.2	2.44
28	SG/ GLP/ A01/ 12/ 02	ආදානාගාර මාර්ගය දෙවන පටුම	225743.257/ 148263.324	225739.555/ 148264.55	225724.557/ 148402.342	225723.435/ 148399.997	180.85	2.6	2.6

අනු අංකය.	පාරේච්ඡි කේතය	පාරේ නම	ආරම්භක බණ්ඩාංක (කළුවල ලංකා)		අවසාන බණ්ඩාංක (කළුවල ශ්‍රී ලංකා)		පාරේ දිග (මීටර්)	පාරේ සාමාන්‍ය පළල (මීටර්)	සංවර්ධිත පළල (මීටර්)
			වම	දකුණ	වම	දකුණ			
29	SG/GLP/A01/12/03	බල්ලපාන උඩබාගේ ටර්පන්ටයින මාර්ගය	22549.734/ 148351.857	22552.076/ 148349.756	225447.437/ 147915.473	225448.129/ 147918.528	578.83	3.04	2.44
30	SG/GLP/A01/12/03/01	ටර්පන්ටයින වත්ත පළමු පටුමග	225495.267/ 148083.514	225492.902/ 148080.768	225448.749/ 148082.265	225448.647/ 148079.467	47.5	2.8	2.44
31	SG/GLP/A01/13	පොතුල්ල මාර්ගය	226136.069/ 148089.287	226135.437/ 148092.268	226490.23/ 148353.591	226487.464/ 148354.982	515.65	3.04	2.44
32	SG/GLP/A01/13/01	කිරිවත්තාව වත්ත මාර්ගය	226254.188/ 148118.481	226256.549/ 148119.59	226440.285/ 148007.229	226442.46/ 148008.652	241.66	2.6	2.44
33	SG/GLP/A01/13/02	පොතුල්ල කනත්ත මාර්ගය	226320.14/ 148149.202	226318.774/ 148148.792	226285.766/ 148273.706	226284.676/ 148273.204	134.57	1.2	0.6
34	SG/GLP/A01/14	කොබ්බෑවල රිදීතොටුව මාර්ගය	226167.406/ 147924.376	226166.656/ 147928.814	228738.993/ 146956.348	228740.775/ 146960.754	2986.24	5.5	3.7
35	SG/GLP/A01/14/01	පහලගම පළමු පටුමග	226329.307/ 147899.396	226326.404/ 147898.404	226286.916/ 147946.963	226287.427/ 147943.966	81.67	3.04	3.04
36	SG/GLP/A01/14/02	හරිගල වත්ත මාර්ගය	226347.272/ 147902.032	226345.521/ 147902.447	226336.687/ 148006.051	226335.315/ 148007.216	122.03	1.8	1.8

අනු අංකය	පාරම් නිකේතය	පාරම් නම	ආරම්භක බණ්ඩාංක (කළමනාකරණ ලංකා)		අවසාන බණ්ඩාංක (කළමනාකරණ ලංකා)		පාරම් දින (මිටර්)	පාරම් සාමාන්‍ය පළල (මිටර්)	සංවර්ධිත පළල (මිටර්)
			වම	දකුණ	වම	දකුණ			
37	SG/ GLP/ A01/ 14/ 03	පහලගම දෙල්ගොල්ල මාර්ගය	226408.338/ 147866.218	226405.478/ 147867.646	226696.626/ 148021.958	226694.301/ 148023.916	384.9	3.04	2.44
38	SG/ GLP/ A01/ 14/ 03/ 01	මද්දුවත්ත මාර්ගය	226434.552/ 147887.213	226431.546/ 147886.743	226456.258/ 147952.127	226453.243/ 147952.52	82.85	3.04	1.8
39	SG/ GLP/ A01/ 14/ 03/ 02	පහලගම උඩතවත්ත මාර්ගය	226615.93/ 147986.54	226613.604/ 147985.707	226568.38/ 147999.908	226568.998/ 147997.548	53.01	2.44	1.8
40	SG/ GLP/ A01/ 14/ 03/ 03	දෙල්ගොල්ල පළමු පවුම	226642.993/ 147978.344	226645.87/ 147977.947	226647.805/ 147923.47	226649.992/ 147925.219	59.82	2.8	2.44
41	SG/ GLP/ A01/ 14/ 04	භිට්තාවත්ත මාර්ගය	226609.886/ 147793.072	226606.707/ 147793.254	226627.226/ 147875.63	226624.217/ 147876.055	90.8	3.04	2.44
42	SG/ GLP/ A01/ 14/ 05	උඩදෙණිය මාර්ගය	226671.506/ 147782.908	226674.408/ 147782.834	226767.207/ 147666.171	226769.938/ 147667.086	178.27	2.44	2.44
43	SG/ GLP/ A01/ 14/ 05/ 01	ගල්දොඹේ මාර්ගය	226662.774/ 147739.13	226664.574/ 147736.623	226600.885/ 147704.909	226601.232/ 147702.494	78.67	2.44	2.44
44	SG/ GLP/ A01/ 14/ 06	ගල්කොටුව මාර්ගය	226691.452/ 147787.318	226688.215/ 147787.449	226712.393/ 147865.962	226709.899/ 147867.702	117.31	3.04	2.44

අනු අංකය.	පාරේච්ඡි කේතය	පාරේ නම	ආරම්භක බැංකු (කළමනාකරණ ලේඛන)		අවසාන බැංකු (කළමනාකරණ ලේඛන)		පාරේ දිග (මීටර්)	පාරේ සාමාන්‍ය පළල (මීටර්)	සංවර්ධිත පළල (මීටර්)
			වම	දකුණ	වම	දකුණ			
45	SG/GLP/A01/ 14/07	කහවගහමුල හේන මාර්ගය	226800.977/ 147783.125	226797.98/ 147783.091	226800.173/ 147846.938	226797.733/ 147846.935	67.21	2.44	2.2
46	SG/GLP/A01/ 14/08	අරබෙවෙල මාර්ගය	226947.539/ 147751.74	226945.36/ 147752.839	226918.234/ 147974.594	226917.737/ 147972.205	336.88	2.44	2.44
47	SG/GLP/A01/ 14/09	වැවේ වත්ත මාර්ගය	227020.495/ 147703.913	227022.945/ 147703.298	227035.051/ 147579.347	227036.787/ 147581.061	130.39	2.44	2.44
48	SG/GLP/A01/ 14/10	දොබදෙණිය වත්ත මාර්ගය	227030.661/ 147706.255	227027.315/ 147706.894	227211.189/ 147735.729	227208.517/ 147736.567	226.43	2.8	2.44
49	SG/GLP/A01/ 14/11	පොල්වත්ත මාර්ගය	227156.151/ 147582.26	227152.835/ 147584.946	227269.415/ 148087.945	227266.134/ 148090.568	601.85	4.2	3.04
50	SG/GLP/A01/ 14/11/01	පිදුම මාර්ගය	227245.975/ 147716.541	227245.014/ 147720.636	227897.861/ 147627.744	227896.699/ 147631.78	715.88	4.2	2.8
51	SG/GLP/A01/ 14/11/01/01	දවදොළ මාර්ගය	227301.562/ 147700.923	227304.63/ 147701.802	227372.518/ 147594.195	227372.272/ 147597.225	158.86	3.04	2.44
52	SG/GLP/A01/ 14/11/01/02	අල්ලේ වත්ත මාර්ගය	227382.121/ 147695.307	227384.483/ 147694.319	227393.544/ 147643.503	227395.733/ 147644.58	55.01	2.44	2.44

අනු අංකය	පාරේඛි කේතය	පාරේ නම	ආරම්භක බණ්ඩාංක (කළමනාකරණ ලංකා)		අවසාන බණ්ඩාංක (කළමනාකරණ ලංකා)		පාරේ දිග (මීටර්)	පාරේ සාමාන්‍ය පළල (මීටර්)	සංවර්ධිත පළල (මීටර්)
			වම	දකුණ	වම	දකුණ			
53	SG/ GLP/ A01/ 14/ 11/ 01/ 03	ආරාම මාර්ගය	227557.794/ 147687.205	227554.635/ 147687.618	227794.308/ 147814.781	227793.937/ 147817.799	312.4	3.04	2.44
54	SG/ GLP/ A01/ 14/ 11/ 01/ 04	පන්විනි මාර්ගය	227610.858/ 147636.759	227614.067/ 147635.716	227627.611/ 147521.939	227625.46/ 147524.088	156.22	3.04	2.44
55	SG/ GLP/ A01/ 14/ 11/ 01/ 05	කිරිවිනිනවිනි මාර්ගය	227840.529/ 147610.42	227843.399/ 147611.466	228015.856/ 147493.072	228016.736/ 147495.981	231.91	3.04	2.44
56	SG/ GLP/ A01/ 14/ 11/ 01/ 05/ 01	පොකුණවල විනි මාර්ගය	227900.073/ 147551.69	227902.54/ 147549.736	227855.025/ 147487.97	227857.585/ 147486.332	79.76	3.04	2.44
57	SG/ GLP/ A01/ 14/ 11/ 02	අගලවිනි මාර්ගය	227191.979/ 147812.938	227192.917/ 147816.619	227308.235/ 147805.629	227308.743/ 147808.627	128.64	3.04	2.44
58	SG/ GLP/ A01/ 14/ 11/ 03	පොල්විනි අරබෙවෙල මාර්ගය	227197.259/ 147916.976	227196.495/ 147914.487	226992.639/ 147841.076	226993.332/ 147838.46	248.78	2.6	2.44
59	SG/ GLP/ A01/ 14/ 12	දිගු ජනපද මාර්ගය	227178.214/ 147559.742	227181.244/ 147557.578	227344.313/ 147395.289	227340.024/ 147395.645	767.24	3.66	2.44
60	SG/ GLP/ A01/ 14/ 12/ 01	දළුගල මාර්ගය	227130.039/ 147410.632	227131.112/ 147407.766	226862.493/ 147447.216	226862.724/ 147444.184	276.58	3.04	2.44

අනු අංකය.	පාරේච්ඡි කේතය	පාරේ නම	ආරම්භක බණ්ඩාංක (කළුවල ලංකා)		අවසාන බණ්ඩාංක (කළුවල ශ්‍රී ලංකා)		පාරේ දිග (මීටර්)	පාරේ සාමාන්‍ය සාළල (මීටර්)	සංවර්ධිත සාළල (මීටර්)
			වම	දකුණ	වම	දකුණ			
61	SG/GLP/A01/ 14/ 12/ 01/ 01	දළුගල වැව වත්ත මාර්ගය	227005.394/ 147416.354	227002.352/ 147416.424	227011.525/ 147496.743	227008.49/ 147496.893	82.14	3.04	2.44
62	SG/GLP/A01/ 14/ 12/ 02	දිගුන පවුමග	227271.333/ 147331.868	227272.881/ 147329.907	227255.772/ 147290.138	227257.969/ 147289.079	47.53	2.44	2.44
63	SG/GLP/A01/ 14/ 13	ගනේවෙල පොකුණුවල මාර්ගය	227855.587/ 147353.697	227852.655/ 147355.376	227888.921/ 147396.058	227886.704/ 147398.14	57.42	3.04	2.44
64	SG/GLP/A01/ 14/ 13/ 01	ගනේවෙල පොකුණුවල අඩි මාර්ගය	227888.253/ 147396.686	227887.374/ 147397.515	227903.155/ 147470.95	227901.962/ 147471.076	77.34	1.2	1
65	SG/GLP/A01/ 14/ 13/ 01/ 01	ගනේවෙල පොකුණුවල මාර්ගය	227903.778/ 147470.957	227901.34/ 147471.067	227881.385/ 147521.353	227880.115/ 147519.269	63.56	2.44	2.44
66	SG/GLP/A01/ 15	අහකියන මාර්ගය	226163.457/ 147871.042	226163.984/ 147867.879	225507.947/ 148086.811	225505.707/ 148084.447	893	3.2	2.44
67	SG/GLP/A01/ 16	එස් ඩබ්ලිව් ආර් ඩී බණ්ඩාරනායක මාර්ගය	226193.387/ 147705.729	226193.163/ 147710.76	226369.336/ 147741.511	226365.799/ 147745.045	189.9	5	2.44
68	SG/GLP/A01/ 16/ 01	බණ්ඩාරනායක මාර්ගය පළමු පවුමග	226278.727/ 147705.045	226281.329/ 147705.225	226278.004/ 147602.787	226280.604/ 147602.768	104.82	2.6	2.44

අනු අංකය	පාරම්පරික නම	පාරම්පරික නම	ආරම්භක බණ්ඩාංක (කළුපිටි ලංකා)		අවසාන බණ්ඩාංක (කළුපිටි ලංකා)		පාරම්පරික දින (වර්ෂ)	පාරම්පරික සාමාන්‍ය ප්‍රමාණ (වර්ෂ)	සංවර්ධන ප්‍රමාණ (වර්ෂ)
			වම	දකුණ	වම	දකුණ			
69	SG/ GLP/ A01/ 16/ 02	බණ්ඩාරනායක මාර්ගය දෙවන පවුම	226285.067/ 147710.735	226282.642/ 147710.419	226281.871/ 147760.262	226279.436/ 147760.105	52.23	2.44	2.44
70	SG/ GLP/ A01/ 17	බල්ලපාන උඩබිමේ ආසියාතික මාර්ගය	226185.319/ 147607.19	226185.485/ 147602.727	224889.935/ 147523.71	224891.182/ 147517.369	1517.4	4.4	2.8
71	SG/ GLP/ A01/ 17/ 01	ශ්‍රී ලංකා මාර්ගය	226049.843/ 147565.519	226046.621/ 147565.663	225448.129/ 147918.528	225450.356/ 147916.321	856.64	3.04	2.44
72	SG/ GLP/ A01/ 17/ 01/ 01	බල්ලපාන උඩබිමේ පළමු පවුම	225976.096/ 147691.949	225973.855/ 147692.988	226005.302/ 147731.563	226003.455/ 147733.157	51.09	2.44	2.44
73	SG/ GLP/ A01/ 17/ 01/ 02	බල්ලපාන දෙවන මාර්ගය	225859.687/ 147741.048	225857.034/ 147740.677	225860.554/ 147789.794	225857.986/ 147790.201	51	2.6	2.44
74	SG/ GLP/ A01/ 17/ 01/ 03	බල්ලපාන කොටිනේ මාර්ගය	225830.68/ 147708.281	225832.965/ 147709.355	225781.564/ 147664.48	225782.298/ 147662.091	79.02	2.5	2.44
75	SG/ GLP/ A01/ 17/ 01/ 04	බල්ලපාන උඩබිමේ දෙවන පවුම	225551.519/ 147858.756	225552.967/ 147856.504	225492.273/ 147855.003	225492.161/ 147852.566	67.04	2.44	2.44
76	SG/ GLP/ A01/ 17/ 02	බල්ලපාන උඩබිමේ කන්ද මාර්ගය	225740.434/ 147577.397	225736.96/ 147577.282	225450.356/ 147916.321	225447.437/ 147915.473	691.51	3.04	2.44

අනු අංකය.	පාරේච්ඡි කේතය	පාරේ නම	ආරම්භක බැංකු (කළමනාකරණ ලංකා)		අවසාන බැංකු (කළමනාකරණ ලංකා)		පාරේ දිග (මීටර්)	පාරේ සාමාන්‍ය පළල (මීටර්)	සංවර්ධිත පළල (මීටර්)
			වම	දකුණ	වම	දකුණ			
77	SG/GLP/A01/ 17/02/01	කාලි දේවාලය මාර්ගය	225717.835/ 147599.716	225714.941/ 147601.375	225708.433/ 147654.081	225706.028/ 147653.668	56.18	2.44	1.8
78	SG/GLP/A01/ 17/02/02	උඩහවන්ත මාර්ගය	225658.576/ 147643.509	225655.435/ 147646.493	225672.555/ 147679.671	225672.811/ 147682.099	58.66	2.44	2.44
79	SG/GLP/A01/ 17/03	ආවාස මාර්ගය	225674.507/ 147451.296	225676.864/ 147454.617	225969.129/ 147175.867	225972.947/ 147174.509	450.17	4	2.44
80	SG/GLP/A01/ 18	බල්ලපාන පහතබාගේ මාර්ගය	226189.859/ 147393.406	226190.73/ 147397.954	227149.999/ 147158.739	227145.353/ 147161.583	1333.83	4.6	3.04
81	SG/GLP/A01/ 18/01	බල්ලපාන පහතබාගේ පළමු පටුමග	226324.764/ 147195.617	226325.385/ 147194.583	226201.673/ 147097.942	226202.871/ 147097.87	177.53	1.2	1.2
82	SG/GLP/A01/ 18/02	ප්‍රජාශාලාව මාර්ගය	226478.055/ 147145.519	226475.986/ 147147.77	226622.806/ 147286.494	226619.768/ 147286.609	266.96	3.04	2.44
83	SG/GLP/A01/ 18/03	බල්ලපාන සියඹලාපිටිය මාර්ගය	226579.815/ 147044.471	226584.158/ 147044.798	226734.488/ 146548.592	226738.641/ 146547.531	663.62	4	2.44
84	SG/GLP/A01/ 18/03/01	පාඨවන්ත ඉදිදනාවල මාර්ගය	226551.64/ 146971.177	226550.736/ 146968.83	226421.373/ 146995.059	226421.087/ 146992.575	150.37	2.5	2.44

අනු අංකය	පාරම්පරික නේතය	පාරම්පරික නම	ආරම්භක බණ්ඩාංක (කදවල ශ්‍රී ලංකා)		අවසාන බණ්ඩාංක (කදවල ශ්‍රී ලංකා)		පාරම්පරික දින (මිටර්)	පාරම්පරික සාමාන්‍ය පළල (මිටර්)	සංවර්ධිත පළල (මිටර්)
			වම	දකුණ	වම	දකුණ			
85	SG/ GLP/ A01/ 18/ 03/ 02	මීරකන්ද මාර්ගය	226552.674/ 146919.735	226552.731/ 146922.539	226811.27/ 146920.625	226809.537/ 146922.697	270.38	2.7	2.7
86	SG/ GLP/ A01/ 18/ 03/ 03	මීගහවත්ත මාර්ගය	226556.936/ 146847.878	226557.654/ 146844.147	226435.755/ 146703.511	226439.369/ 146702.928	211.7	3.66	2.44
87	SG/ GLP/ A01/ 18/ 03/ 03/ 01	මීගහවත්ත පළමු පටුම	226472.495/ 146770.763	226474.778/ 146774.138	226507.159/ 146763.671	226508.675/ 146766.025	39.11	2.8	2.44
88	SG/ GLP/ A01/ 18/ 03/ 04	සියඹලාපිටිය 6 වැනි පටුම	226578.379/ 146816.723	226581.418/ 146816.48	226573.427/ 146768.712	226576.414/ 146768.143	50.54	3.04	2.44
89	SG/ GLP/ A01/ 18/ 03/ 05	සියඹලාපිටිය 5 වන පටුම	226723.992/ 146686.11	226722.138/ 146688.522	226760.518/ 146802.887	226760.33/ 146799.854	156.61	3.04	2.44
90	SG/ GLP/ A01/ 18/ 03/ 06	සියඹලාපිටිය 4 වන පටුම	226785.887/ 146640.626	226783.472/ 146642.622	226835.132/ 146682.147	226832.886/ 146684.196	66.69	3.04	2.44
91	SG/ GLP/ A01/ 18/ 03/ 07	සියඹලාපිටිය 3 වන පටුම	226791.59/ 146582.334	226793.326/ 146585.163	226916.127/ 146548.557	226916.853/ 146551.51	145.11	3.04	2.44
92	SG/ GLP/ A01/ 18/ 03/ 07/ 01	සියඹලාපිටිය 3 වන පටුම පළමු මාර්ගය	226876.534/ 146576.895	226875.251/ 146580.219	226914.418/ 146572.25	226914.56/ 146574.946	41	2.7	2.44

අනු අංකය.	පාරේච්ඡි කේතය	පාරේ නම	ආරම්භක බිඳ්ඩිංක (කඳවල ලංකා)		අවසාන බිඳ්ඩිංක (කඳවල ලංකා)		පාරේ දිග (මීටර්)	පාරේ සාමාන්‍ය පළල (මීටර්)	සංවර්ධිත පළල (මීටර්)
			වම	දකුණ	වම	දකුණ			
93	SG/GLP/A01/ 18/04	උපාසක චන්ද්‍ර මාර්ගය	226639.031/ 147082.61	226642.007/ 147083.236	226663.789/ 146996.286	226666.738/ 146997.028	93.42	3.04	2.44
94	SG/GLP/A01/ 18/05	පොල්මේන මාර්ගය	226859.046/ 147016.779	226862.164/ 147016.892	226929.521/ 146882.353	226931.162/ 146884.912	167.97	3.04	2.44
95	SG/GLP/A01/ 18/06	බතලකොටුව මාර්ගය	226904.57/ 147025.785	226900.898/ 147025.18	227167.3/ 147108.179	227169.159/ 147110.791	378.79	3.04	2.44
96	SG/GLP/A01/ 19	නො 03 චන්ද්‍ර මාර්ගය	226124.506/ 147111.072	226123.676/ 147106.862	225562.906/ 146991.284	225566.181/ 146993.914	717.73	4.2	2.8
97	SG/GLP/A01/ 19/01	ගුරුමේචන්ද්‍ර මාර්ගය	226058.578/ 147098.002	226055.138/ 147095.556	225022.52/ 147506.768	225018.307/ 147506.723	1351.29	4.2	2.44
98	SG/GLP/A01/ 19/01/01	වෙත්දේසිචන්ද්‍ර දෙවන පටුම	225814.045/ 147178.829	225816.452/ 147177.394	225934.225/ 147060.229	225935.063/ 147063.01	212.94	2.8	2.44
99	SG/GLP/A01/ 19/01/01/01	වෙත්දේසිචන්ද්‍ර දෙවන පටුම පළමු මාර්ගය	225833.404/ 147103.831	225835.989/ 147102.607	225778.963/ 147095.952	225779.122/ 147093.156	64.99	2.8	2.44
100	SG/GLP/A01/ 19/01/02	ගුරුමේචන්ද්‍ර පළමු පටුම	225735.1/ 147200.246	225737.847/ 147199.848	225691.239/ 147104.441	225693.462/ 147103.297	120.34	2.5	2.44

අනු අංකය	පාරම්පරික කේතය	පාරේ නම	ආරම්භක බණ්ඩාංක (කළමනාකරණ ලංකා)		අවසාන බණ්ඩාංක (කළමනාකරණ ලංකා)		පාරේ දිග (මීටර්)	පාරේ සාමාන්‍ය පළල (මීටර්)	සංවර්ධිත පළල (මීටර්)
			වම	දකුණ	වම	දකුණ			
101	SG/ GLP/ A01/ 19/ 02	වෙනදේසිවත්ත පළමු පවුම	225951.761/ 147047.385	225948.95/ 147045.212	225891.03/ 147182.802	225887.025/ 147181.93	180.43	3.4	2.44
102	SG/ GLP/ A01/ 20	පහලවත්ත මාර්ගය	226082.895/ 146877.167	226082.51/ 146874.722	225940.337/ 146927.252	225940.254/ 146924.813	167.02	2.44	2.44
103	SG/ GLP/ A01/ 21	පල්ලේවිට්ටිවත්ත මාර්ගය	226088.195/ 146832.559	226088.734/ 146837.587	226564.841/ 146645.785	226561.073/ 146649.072	649.23	5	2.44
104	SG/ GLP/ A01/ 21/ 01	නිවාස සංකීර්ණය මාර්ගය	226187.831/ 146793.37	226185.532/ 146795.378	226346.897/ 146963.076	226344.715/ 146965.193	235.26	3.04	2.44
105	SG/ GLP/ A01/ 21/ 02	පල්ලේවිට්ටිවත්ත පළමු පවුම	226300.323/ 146648.627	226300.739/ 146651.053	226407.964/ 146657.694	226407.659/ 146660.115	110.72	2.44	2.44
106	SG/ GLP/ A01/ 21/ 03	පල්ලේවිට්ටිවත්ත දෙවන පවුම	226282.52/ 146612.969	226282.823/ 146610.544	226275.287/ 146516.703	226277.482/ 146517.769	128.87	2.44	2.44
107	SG/ GLP/ A01/ 21/ 04	පල්ලේවිට්ටිවත්ත 3 වන පවුම	226309.805/ 146607.61	226313.511/ 146608.092	226310.813/ 146559.755	226311.109/ 146556.729	87.9	3.04	2.44
108	SG/ GLP/ A01/ 22	මෙහිල්ල මාර්ගය	226075.771/ 146805.115	226075.801/ 146801.914	225927.075/ 146803.813	225927.754/ 146800.685	156.02	3.2	2.6


අනු අංකය.	පාරේච්ඡි කේතය	පාරේ නම	ආරම්භක බණ්ඩාංක (කළුවල ලංකා)		අවසාන බණ්ඩාංක (කළුවල ශ්‍රී ලංකා)		පාරේ දිග (මීටර්)	පාරේ සාමාන්‍ය පළල (මීටර්)	සංවර්ධිත පළල (මීටර්)
			වම	දකුණ	වම	දකුණ			
109	SG/GLP/A01/ 22/01	මෙහිල්ල පවුම	226033.076/ 146806.03	226030.364/ 146806.8	225926.463/ 146841.178	225926.292/ 146838.583	134.6	2.6	2.44
110	SG/GLP/A01/ 23	අඹන්පිටියවත්ත මාර්ගය	226077.375/ 146762.571	226077.584/ 146759.15	225787.863/ 146786.676	225788.053/ 146783.281	320.06	3.4	2.44
111	SG/GLP/A01/ 23/01	අඹන්පිටියවත්ත පවුම	225940.637/ 146753.652	225944.322/ 146752.087	225883.413/ 146684.641	225886.509/ 146684.494	115.18	3.1	2.44
112	SG/GLP/A01/ 24	කර්මන්තපුර මාර්ගය	226082.318/ 146690.676	226082.657/ 146684.598	225915.913/ 146630.942	225921.188/ 146633.8	263.99	6	5.2
113	SG/GLP/A01/ 25	මහදෙණියවත්ත මාර්ගය	226089.699/ 146550.769	226089.992/ 146545.575	225267.38/ 146464.195	225262.281/ 146465.21	970.14	5.2	3.66
114	SG/GLP/A01/ 25/01	මෙහිල්ල වත්ත පළමු පවුම	225895.088/ 146523.691	225891.208/ 146521.898	225769.74/ 146648.416	225766.809/ 146649.224	226.89	3.04	2.44
115	SG/GLP/A01/ 25/02	මෙහිල්ල වත්ත දෙවන පවුම	225851.818/ 146489.955	225854.228/ 146491.292	225775.333/ 146400.74	225776.032/ 146398.224	191.9	2.6	2.44
116	SG/GLP/A01/ 25/03	මහදෙණියවත්ත පළමු පවුම	225336.356/ 146434.831	225339.512/ 146435.362	225375.616/ 146296.041	225378.531/ 146296.903	150.17	3.04	2.44


අනු අංකය	පාරම්පරික කේතය	පාර්ශ්ව නම	ආරම්භක බණ්ඩාංක (කළමනාකරණ ලංකා)		අවසාන බණ්ඩාංක (කළමනාකරණ ලංකා)		පාර්ශ්ව දිග (මීටර්)	පාර්ශ්ව භාවිතය (මීටර්)	සංවර්ධන ප්‍රදේශ (මීටර්)
			වම	දකුණ	වම	දකුණ			
117	SG/ GLP/ A01/ 25/ 04	නො 03 වත්ත මාර්ගය	225259.968/ 146441.27	225260.646/ 146437.925	225539.07/ 147013.709	225541.489/ 147015.594	1072.19	3.04	2
118	SG/ GLP/ A01/ 26	බල්ලපාන පළමු පටුම	226104.977/ 146385.216	226105.783/ 146382.266	226019.44/ 146397.081	226019.053/ 146394.066	93.71	3.04	2.44
119	SG/ GLP/ A01/ 27	බල්ලපාන දෙවන පටුම	226106.155/ 146380.985	226107.188/ 146377.256	226061.53/ 146253.7	226065.011/ 146254.833	146.63	3.66	2.44
120	SG/ GLP/ A01/ 28	සියඹලාපිටිය දමමල මාර්ගය	226190.455/ 146246	226189.127/ 146250.699	227715.297/ 146536.79	227716.562/ 146541.401	2021.89	4.7	2.44
121	SG/ GLP/ A01/ 28/ 01	සියඹලාපිටිය පළමු පටුම	226285.189/ 146243.887	226286.99/ 146245.649	226444.042/ 146284.236	226441.908/ 146285.538	212.31	2.5	2.44
122	SG/ GLP/ A01/ 28/ 02	සියඹලාපිටිය දෙවන පටුම	226409.13/ 146411.732	226410.691/ 146413.705	226452.743/ 146359.689	226455.132/ 146360.427	74.62	2.5	2.44
123	SG/ GLP/ A01/ 28/ 03	යහලොන්න විහාර මාර්ගය	226505.925/ 146480.536	226509.604/ 146481.022	226566.069/ 145582.315	226569.939/ 145581.543	1325.41	3.66	2.44
124	SG/ GLP/ A01/ 28/ 03/ 01	සියඹලාපිටිය වෙලමඩ මාර්ගය	226569.168/ 146377.171	226567.693/ 146379.487	226767.811/ 146096.784	226768.702/ 146094.5	553.97	2.44	2.44


අනු අංකය.	පාරේච්ඡි කේතය	පාරේ නම	ආරම්භක බිඳ්ඩොංක (කළුවල ලංකා)		අවසාන බිඳ්ඩොංක (කළුවල ශ්‍රී ලංකා)		පාරේ දිග (මීටර්)	පාරේ සාමාන්‍ය පළල (මීටර්)	සංවර්ධිත පළල (මීටර්)
			වම	දකුණ	වම	දකුණ			
125	SG/GLP/A01/ 28/ 04	ගෙවල් 10 මාර්ගය	227648.881/ 146485.267	227647.135/ 146483.452	227546.77/ 146541.76	227546.419/ 146539.346	119.72	2.44	2.44
126	SG/GLP/A01/ 29	යටාලනිස්ස ධර්මායතනය මාර්ගය	226218.491/ 146047.505	226218.112/ 146050.529	226275.78/ 145998.932	226278.518/ 146000.253	99.96	3.04	2.6
127	SG/GLP/A01/ 29/ 01	නිශ්ශංකගේන මාර්ගය	226261.195/ 146048.933	226258.581/ 146050.5	226451.179/ 146087.961	226448.929/ 146090.006	204.51	3.04	2.44
128	SG/GLP/A01/ 30	කළුගඟගේන මාර්ගය	226209.238/ 146024.075	226209.596/ 146021.05	225457.815/ 146476.962	225455.941/ 146474.526	1088.01	3.04	2.44
129	SG/GLP/A01/ 30/ 01	යට්ටෝගොඩ පවුමග	226163.957/ 146035.022	226165.788/ 146032.58	226135.646/ 146007.465	226138.661/ 146007.859	45.96	3.04	2.44
130	SG/GLP/A01/ 30/ 02	කළුගඟගේන පළමු පවුමග	226066.231/ 146094.347	226064.485/ 146094.789	225984.961/ 146174.673	225984.437/ 146172.949	134.7	1.8	1.8
131	SG/GLP/A01/ 30/ 03	කළුගඟගේන ගම්මැද මාර්ගය	225490.45/ 146418.828	225489.489/ 146422.153	225756.447/ 146415.63	225755.141/ 146412.918	559.41	3.1	2.44
132	SG/GLP/A01/ 31	කෘෂිකර්ම සේවා මධ්‍යස්ථාන මාර්ගය	226224.243/ 145905.022	226224.652/ 145909.021	226271.25/ 145841.75	226275.25/ 145841.824	99.47	4	3.66


අනු අංකය	පාරම්පරික කේතය	පාර්ශ්ව නම	ආරම්භක බණ්ඩාංක (කළමනාකරණ ලංකා)		අවසාන බණ්ඩාංක (කළමනාකරණ ලංකා)		පාර්ශ්ව දිග (මීටර්)	පාර්ශ්ව සාමාන්‍ය පළල (මීටර්)	සංවර්ධිත පළල (මීටර්)
			වම	දකුණ	වම	දකුණ			
133	SG/ GLP/ A01/ 32	මොණරකන්ද මාර්ගය	226195.476/ 145782.619	226195.075/ 145779.567	225427.466/ 145947.028	225426.781/ 145944.066	827.54	3.04	2.5
134	SG/ GLP/ A01/ 32/ 01	ගල්ගොඩගේන ඉහළ කොටස මාර්ගය	225935.742/ 145838.886	225931.159/ 145838.242	225912.186/ 145940.796	225909.435/ 145939.502	120.68	3.04	2.44
135	SG/ GLP/ A01/ 33	යට්ටේගොඩ ඉහළගම මාර්ගය	226188.561/ 145635.995	226189.343/ 145631.045	225353.32/ 145733.451	225349.369/ 145738.456	927.31	5	2.44
136	SG/ GLP/ A01/ 33/ 01	කපුකොටුව මාර්ගය	226133.656/ 145622.673	226131.422/ 145620.596	226033.503/ 145711.499	226031.76/ 145709.007	142.98	3.04	2.44
137	SG/ GLP/ A01/ 33/ 02	දම්රාජ විහාර මාර්ගය	226077.044/ 145571.417	226074.463/ 145572.567	226009.851/ 145551.907	226007.829/ 145550.118	87.99	2.7	2.44
138	SG/ GLP/ A01/ 33/ 02/ 01	දම්රාජ විහාර පළමු පටුම	226036.501/ 145537.188	226038.983/ 145537.673	226091.62/ 145376.761	226094.069/ 145376.257	190.48	2.5	2.44
139	SG/ GLP/ A01/ 33/ 02/ 02	දම්රාජ විහාර දෙවන පටුම	226033.632/ 145537.084	226036.157/ 145537.15	225998.045/ 145499.536	226000.448/ 145498.848	57.83	2.5	2.44
140	SG/ GLP/ A01/ 33/ 02/ 03	දම්රාජ විහාර 3 වන පටුම	226010.886/ 145546.662	226013.087/ 145544.064	225943.612/ 145520.886	225945.17/ 145518.681	79.04	2.7	2.44


අනු අංකය.	පාරේහි කේතය	පාරේ නම	ආරම්භක බිඳ්ඩංක (කළුවල ලංකා)		අවසාන බිඳ්ඩංක (කළුවල ලංකා)		පාරේ දිග (මීටර්)	පාරේ සාමාන්‍ය පළල (මීටර්)	සංවර්ධිත පළල (මීටර්)
			වම	දකුණ	වම	දකුණ			
141	SG/GLP/A01/ 33/03	පන්නි දේවාල මාර්ගය	225882.653/ 145624.325	225879.577/ 145623.107	225611.574/ 145786.378	225611.096/ 145783.215	348.11	3.2	2.6
142	SG/GLP/A01/ 33/04	යට්ටේගොඩ කන්ද මාර්ගය	225748.212/ 145619.611	225751.247/ 145618.676	225565.103/ 145246.275	225566.464/ 145243.558	738.43	3.04	2.44
143	SG/GLP/A01/ 34	දොරොඩිව මාර්ගය	226202.197/ 145625.872	226201.437/ 145631.06	226913.899/ 145285.806	226918.474/ 145288.277	1000.88	5.2	3.66
144	SG/GLP/A01/ 34/01	නේ වත්ත මාර්ගය	226238.711/ 145627.297	226235.439/ 145627.442	226446.868/ 145679.661	226449.856/ 145680.806	271.42	3.2	2.44
145	SG/GLP/A01/ 35	කෙහෙල්හේන වත්ත මාර්ගය	226220.676/ 144981.817	226221.036/ 144978.796	226157.405/ 144956.72	226156.555/ 144953.801	79.13	3.04	3.04
146	SG/GLP/A01/ 36	පලපොලුව මාර්ගය	226197.438/ 144654.338	226198.159/ 144657.819	226615.633/ 144571.465	226618.064/ 144573.469	449.69	3.04	2.44
147	SG/GLP/A01/ 36/01	පලපොලුව පළමු පටුම	226270.553/ 144607.222	226272.92/ 144608.041	226299.695/ 144548.322	226302.13/ 144548.892	69.12	2.5	2.44

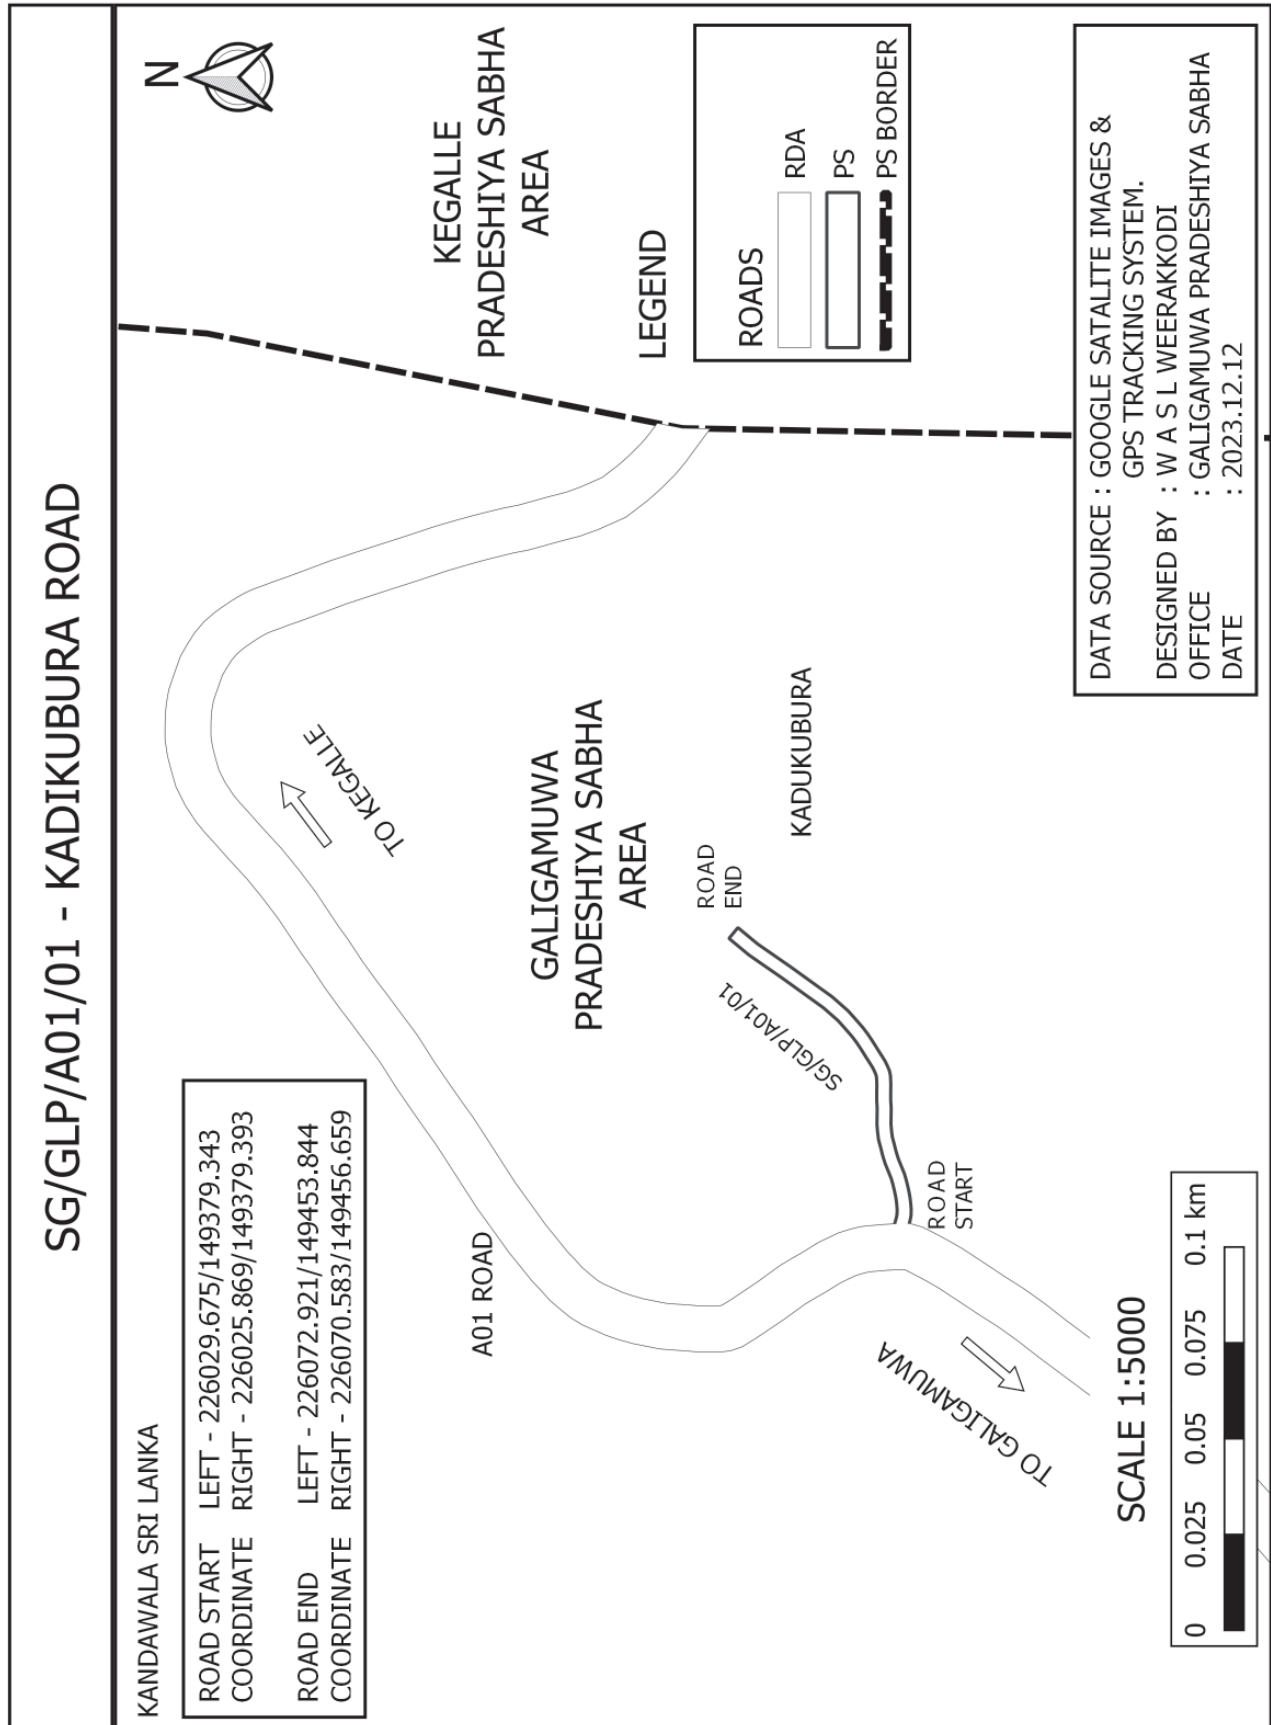


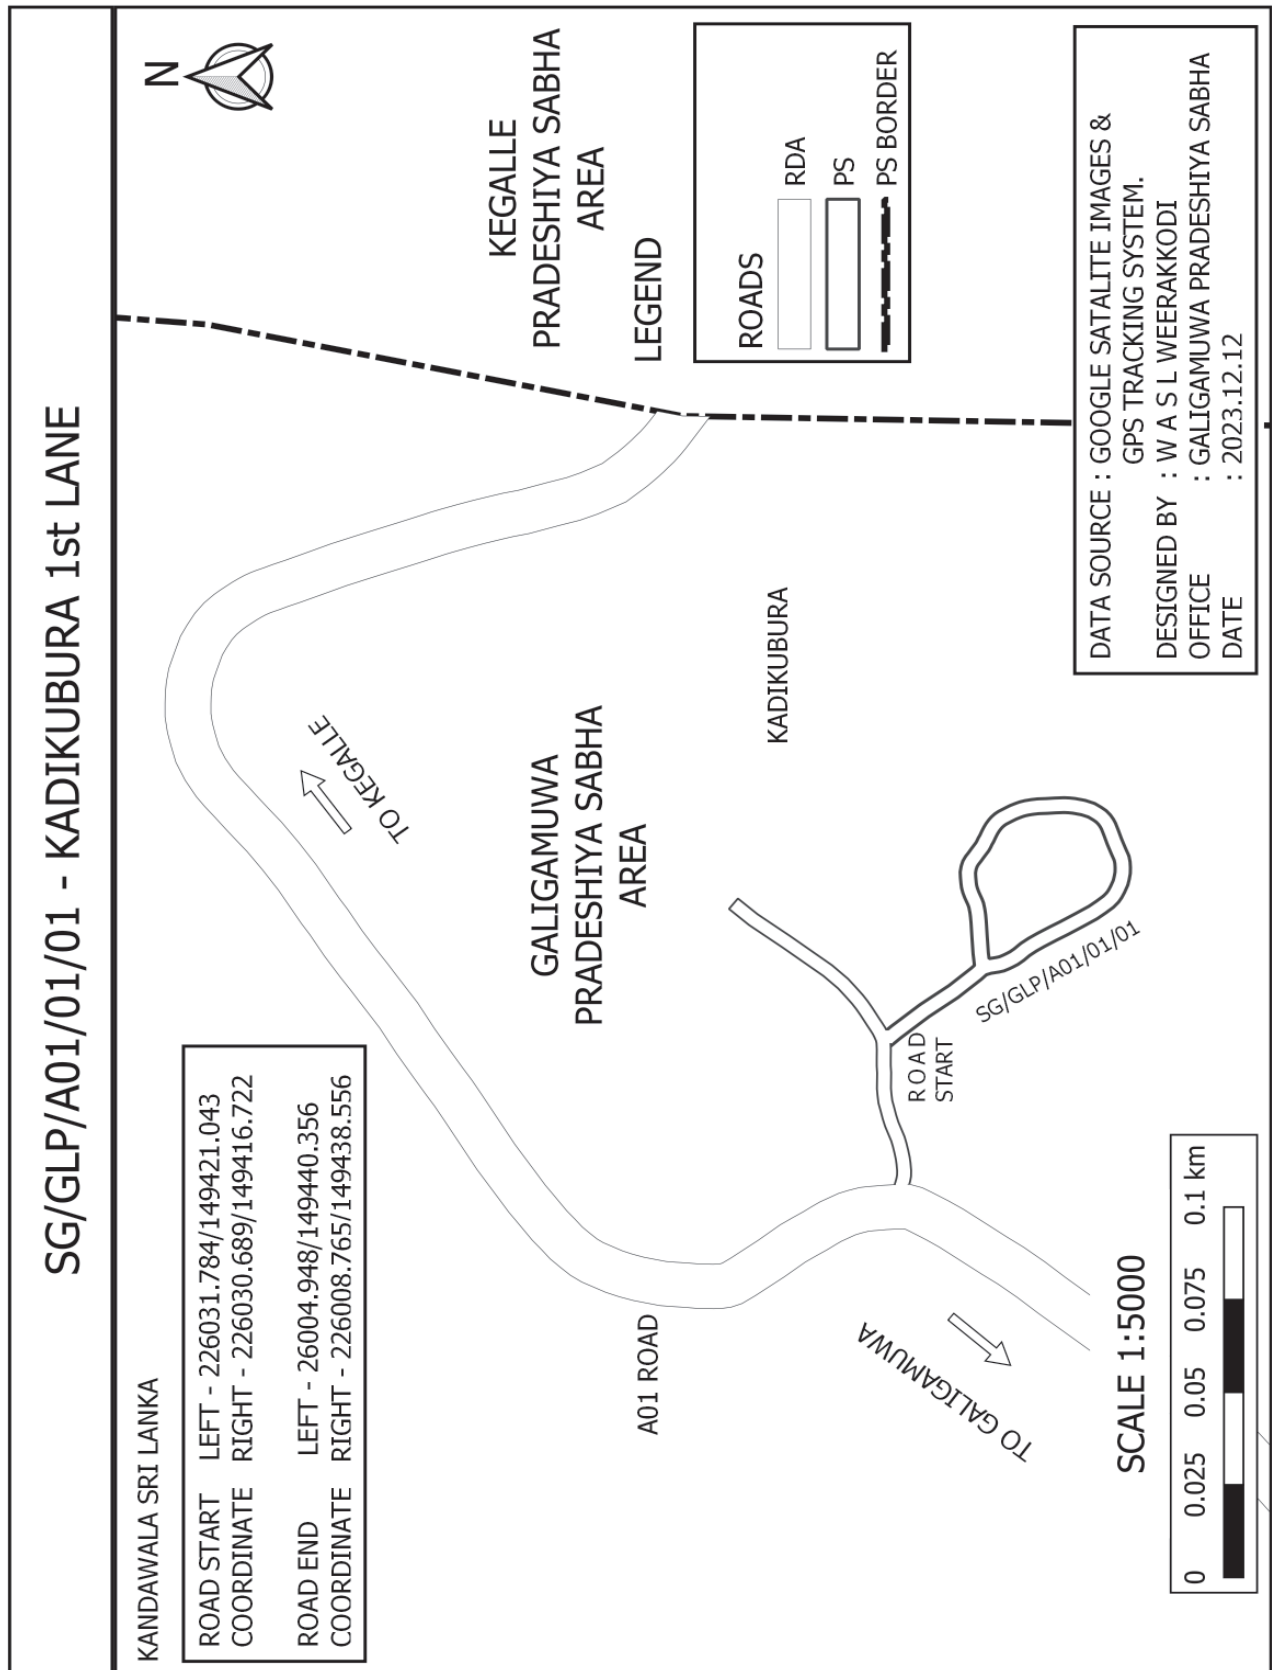


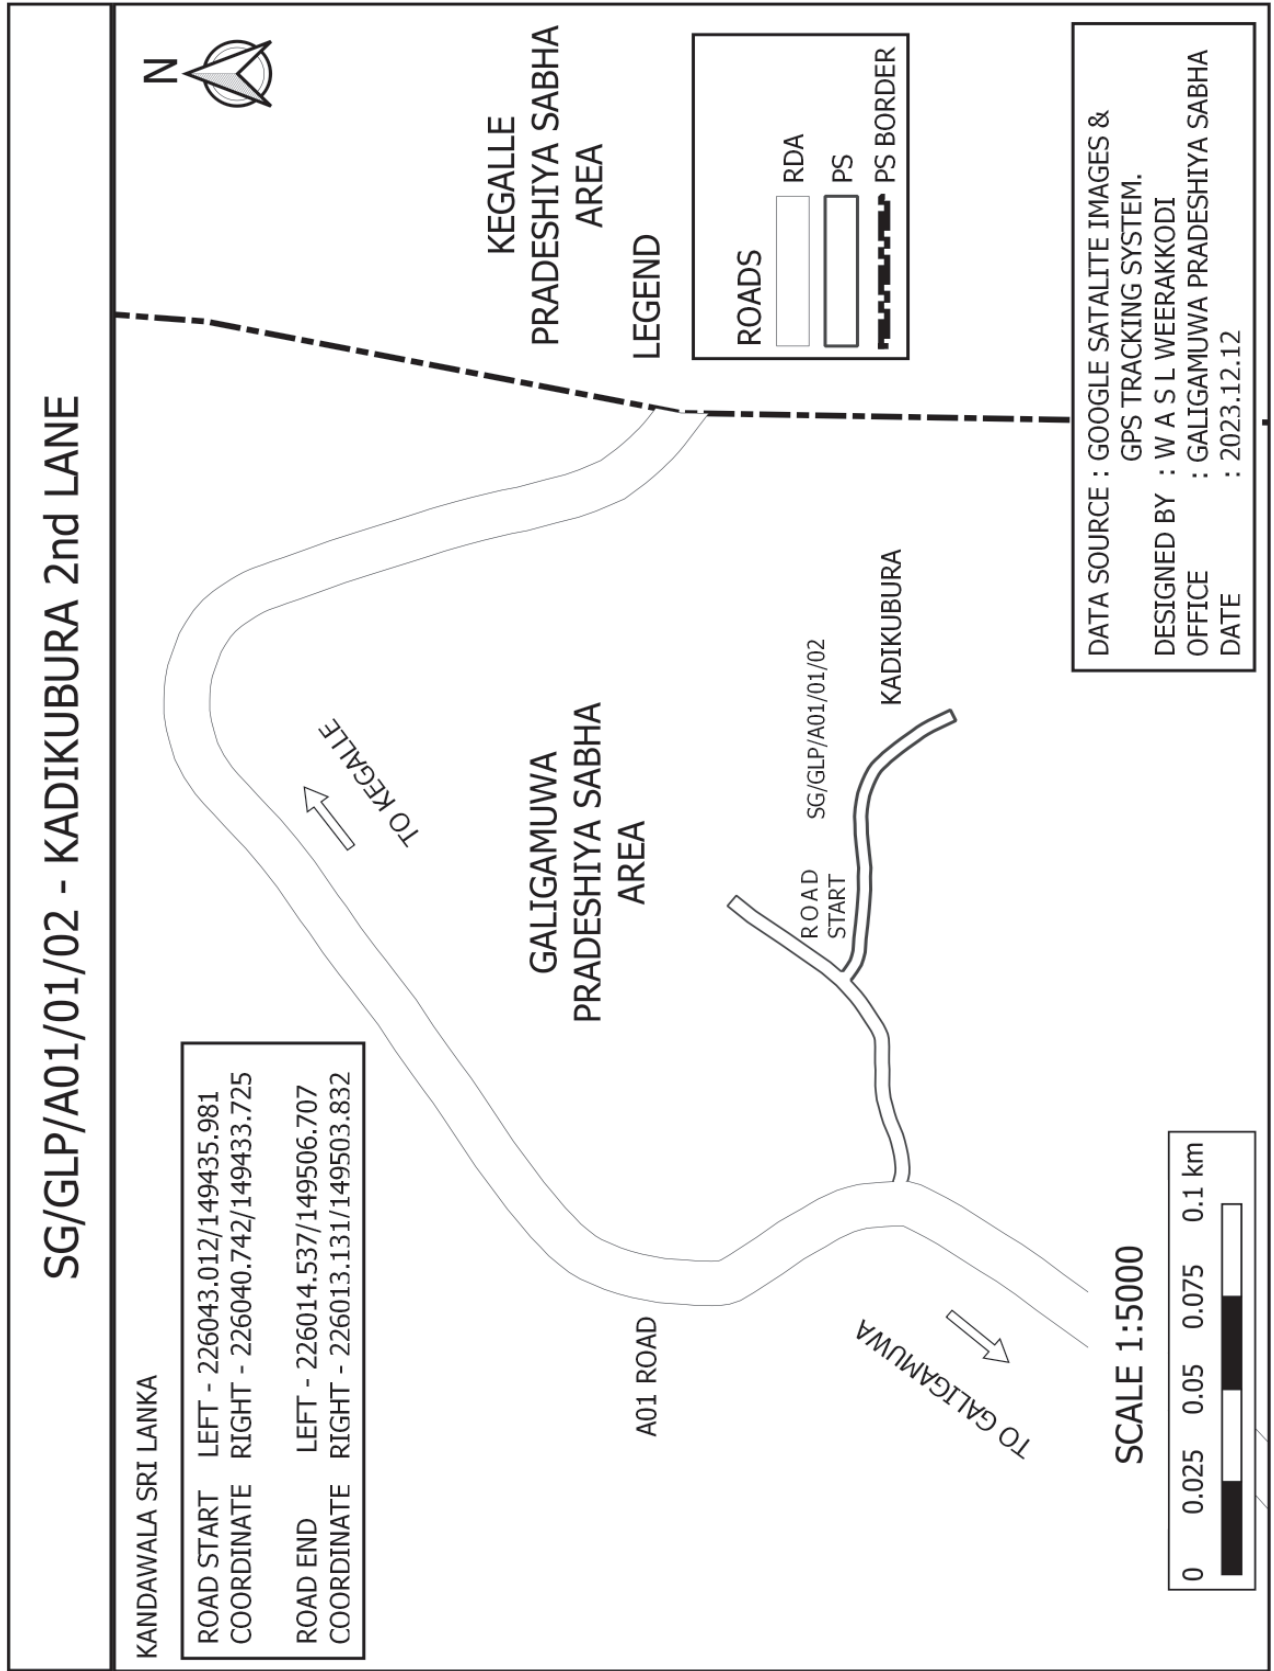


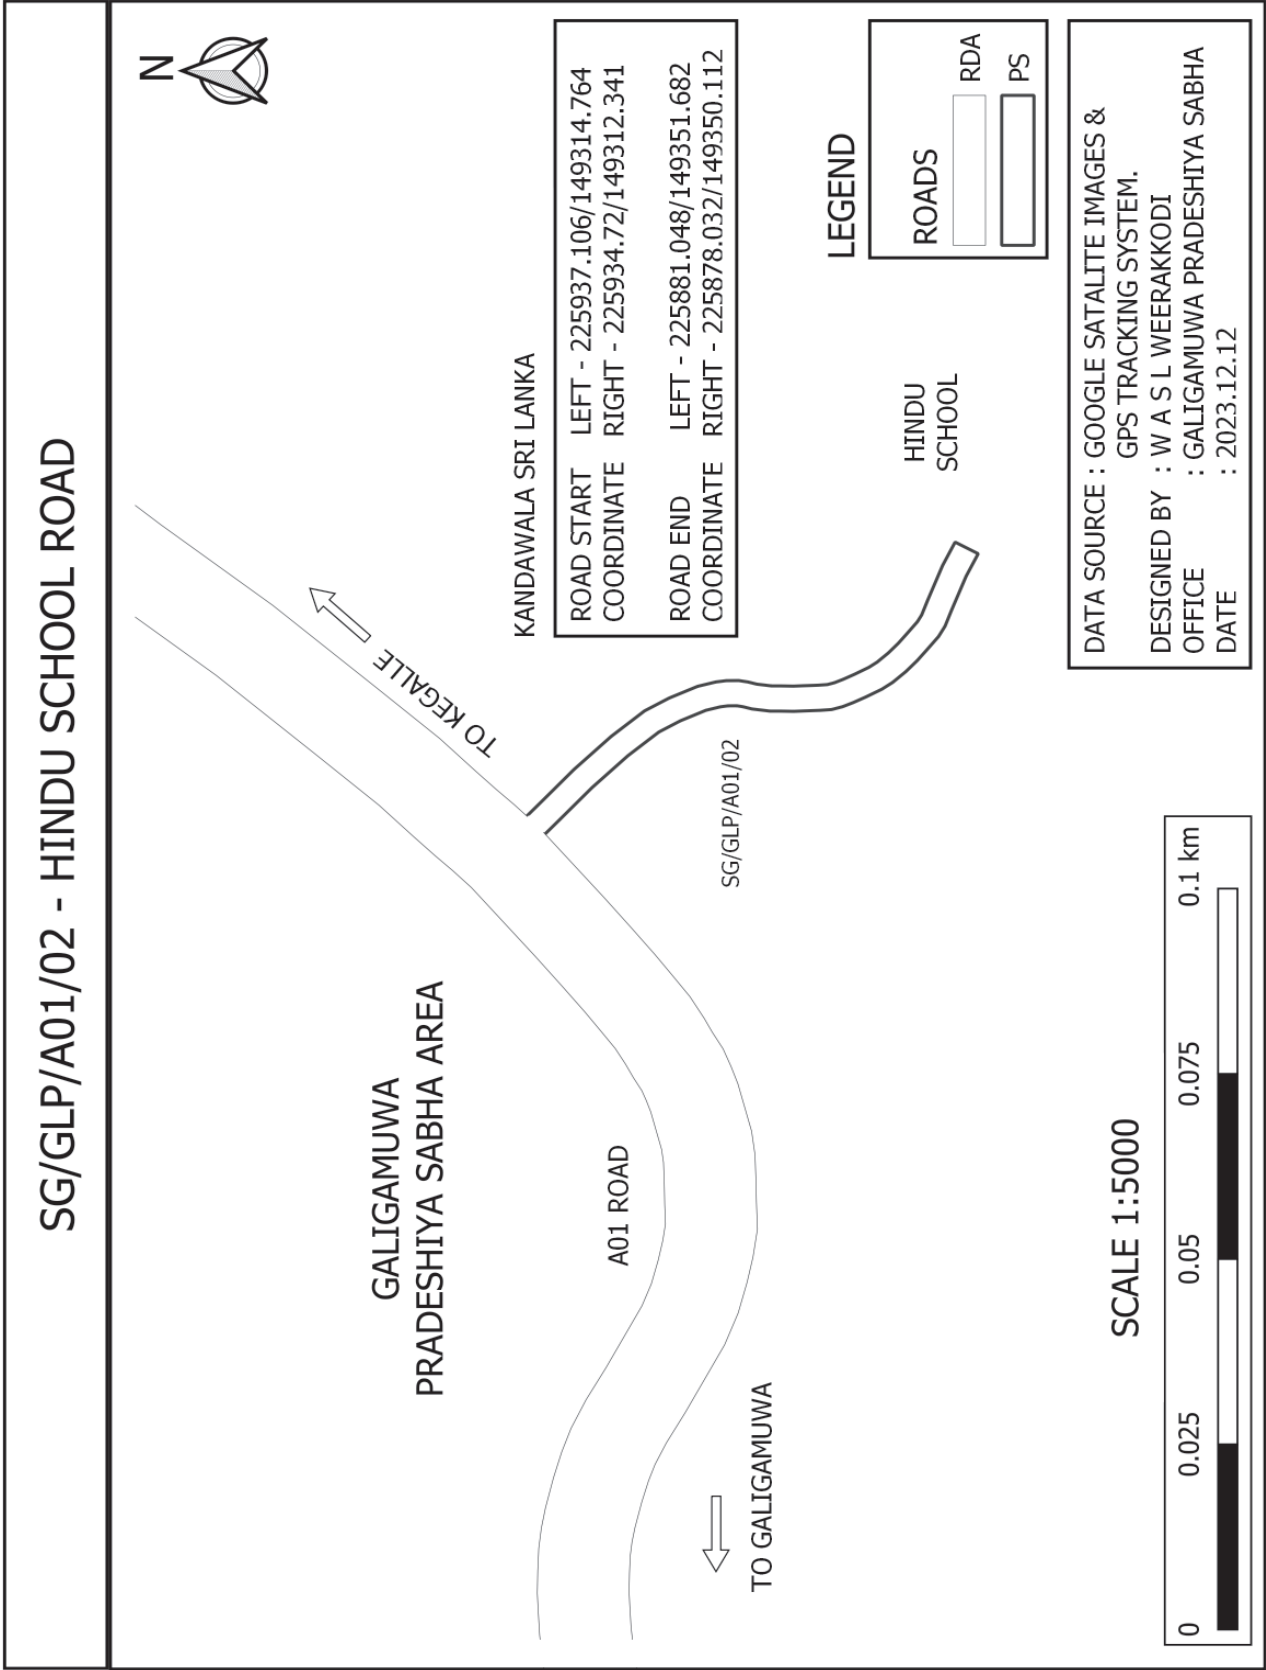


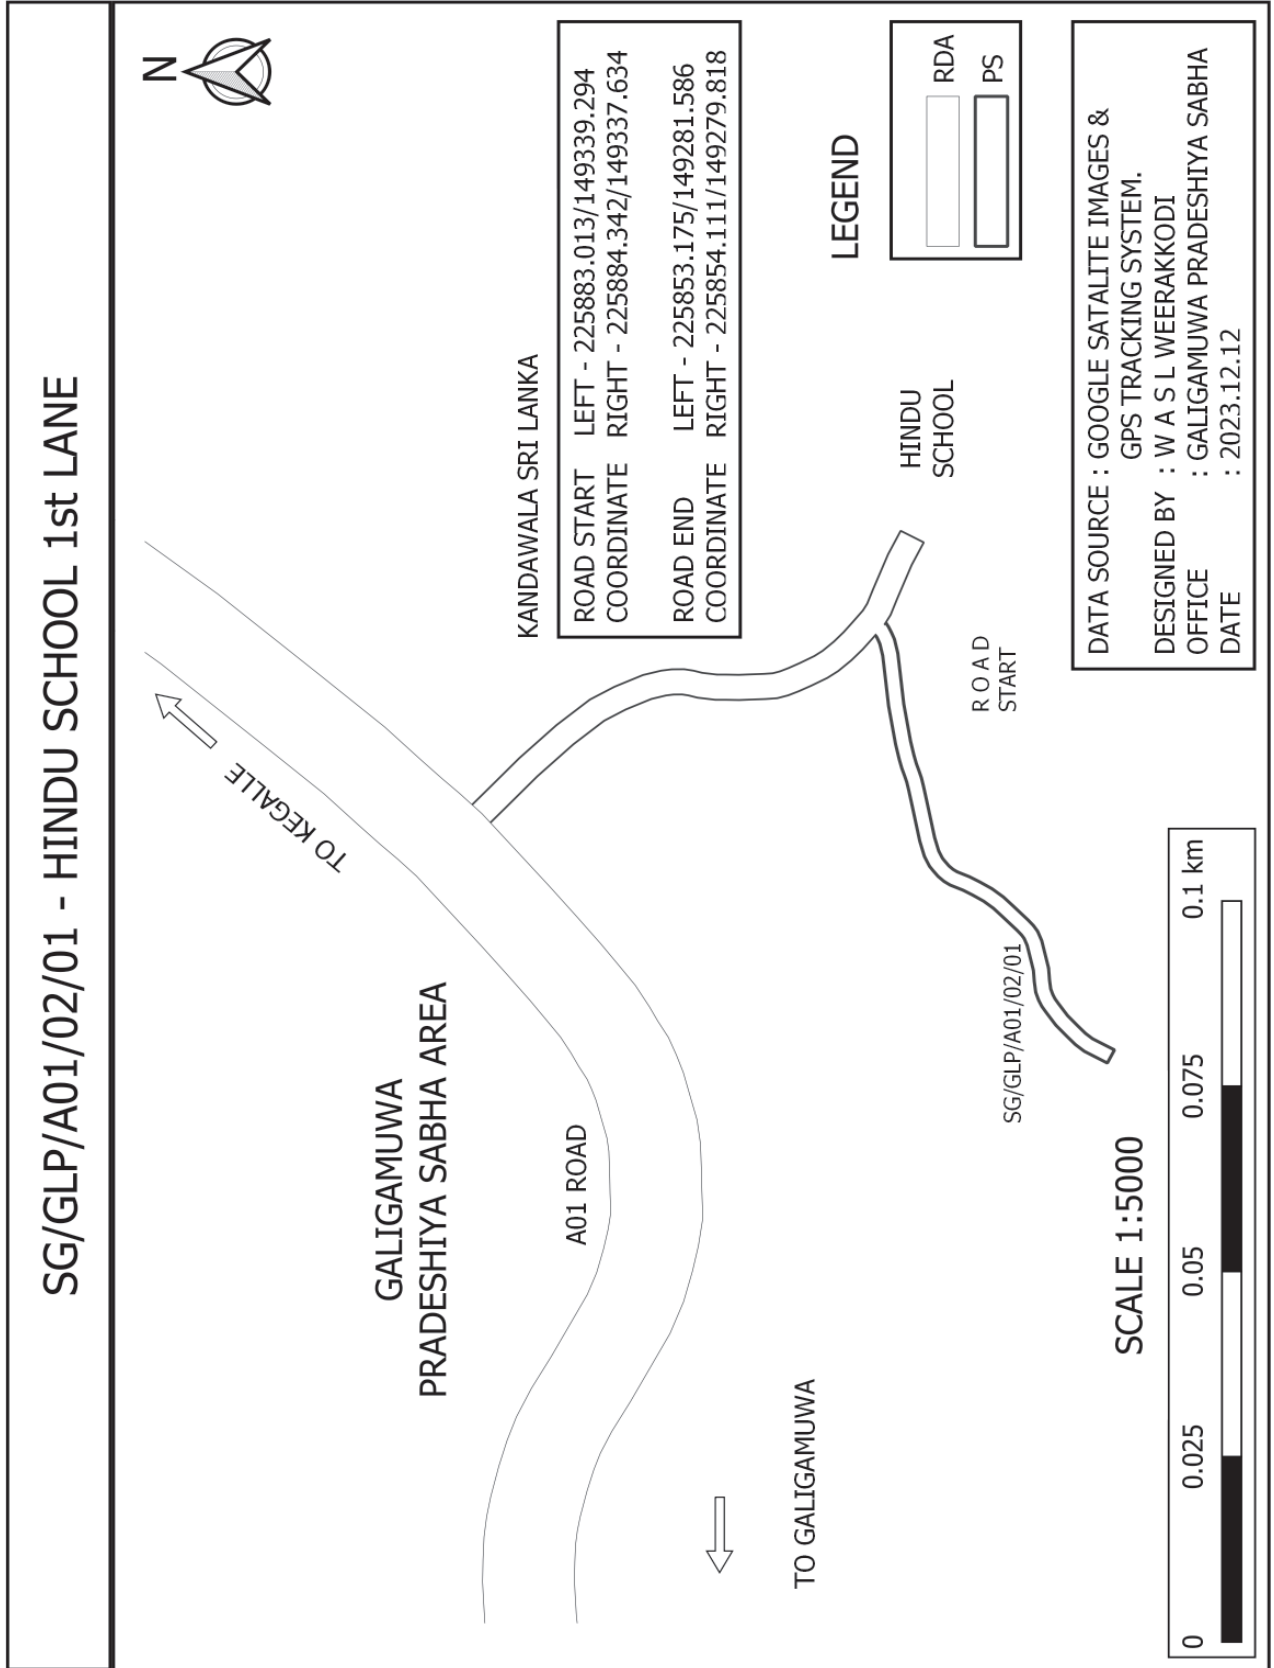


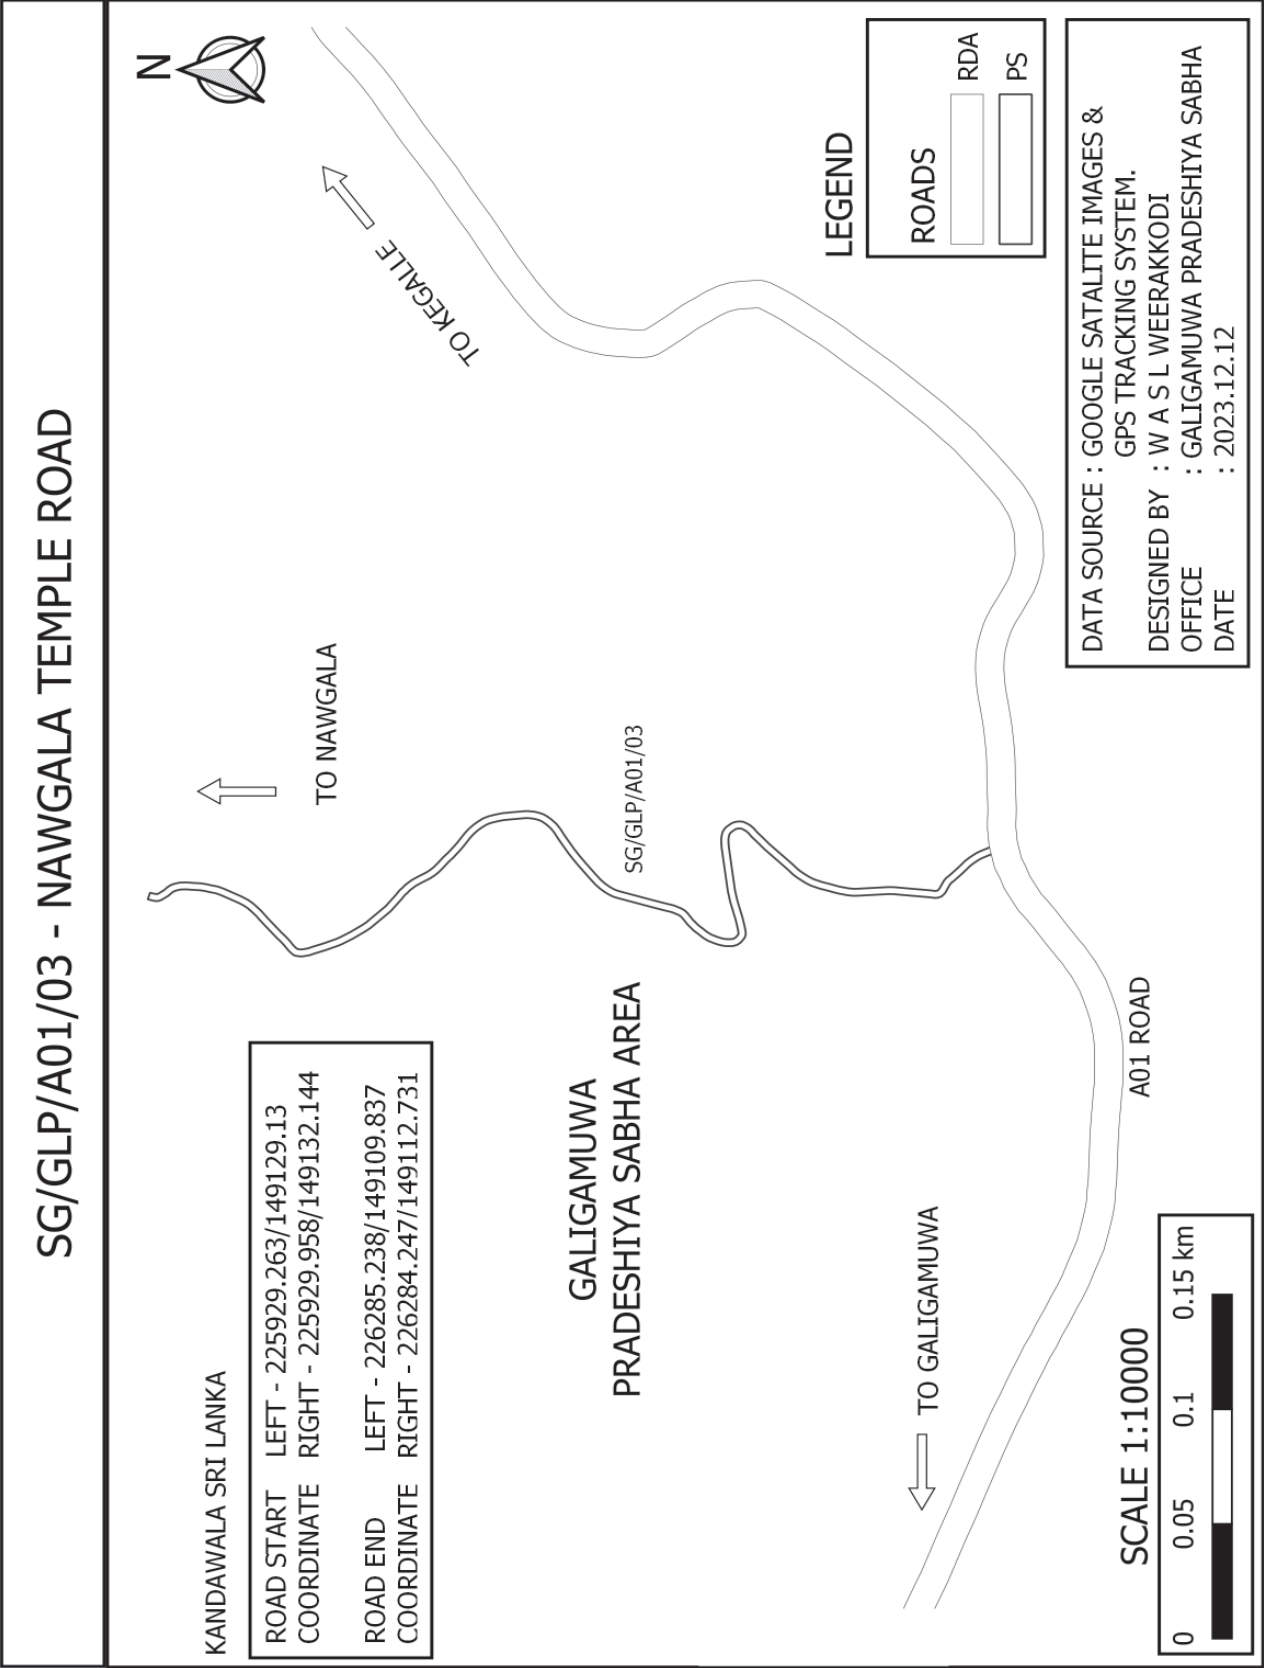


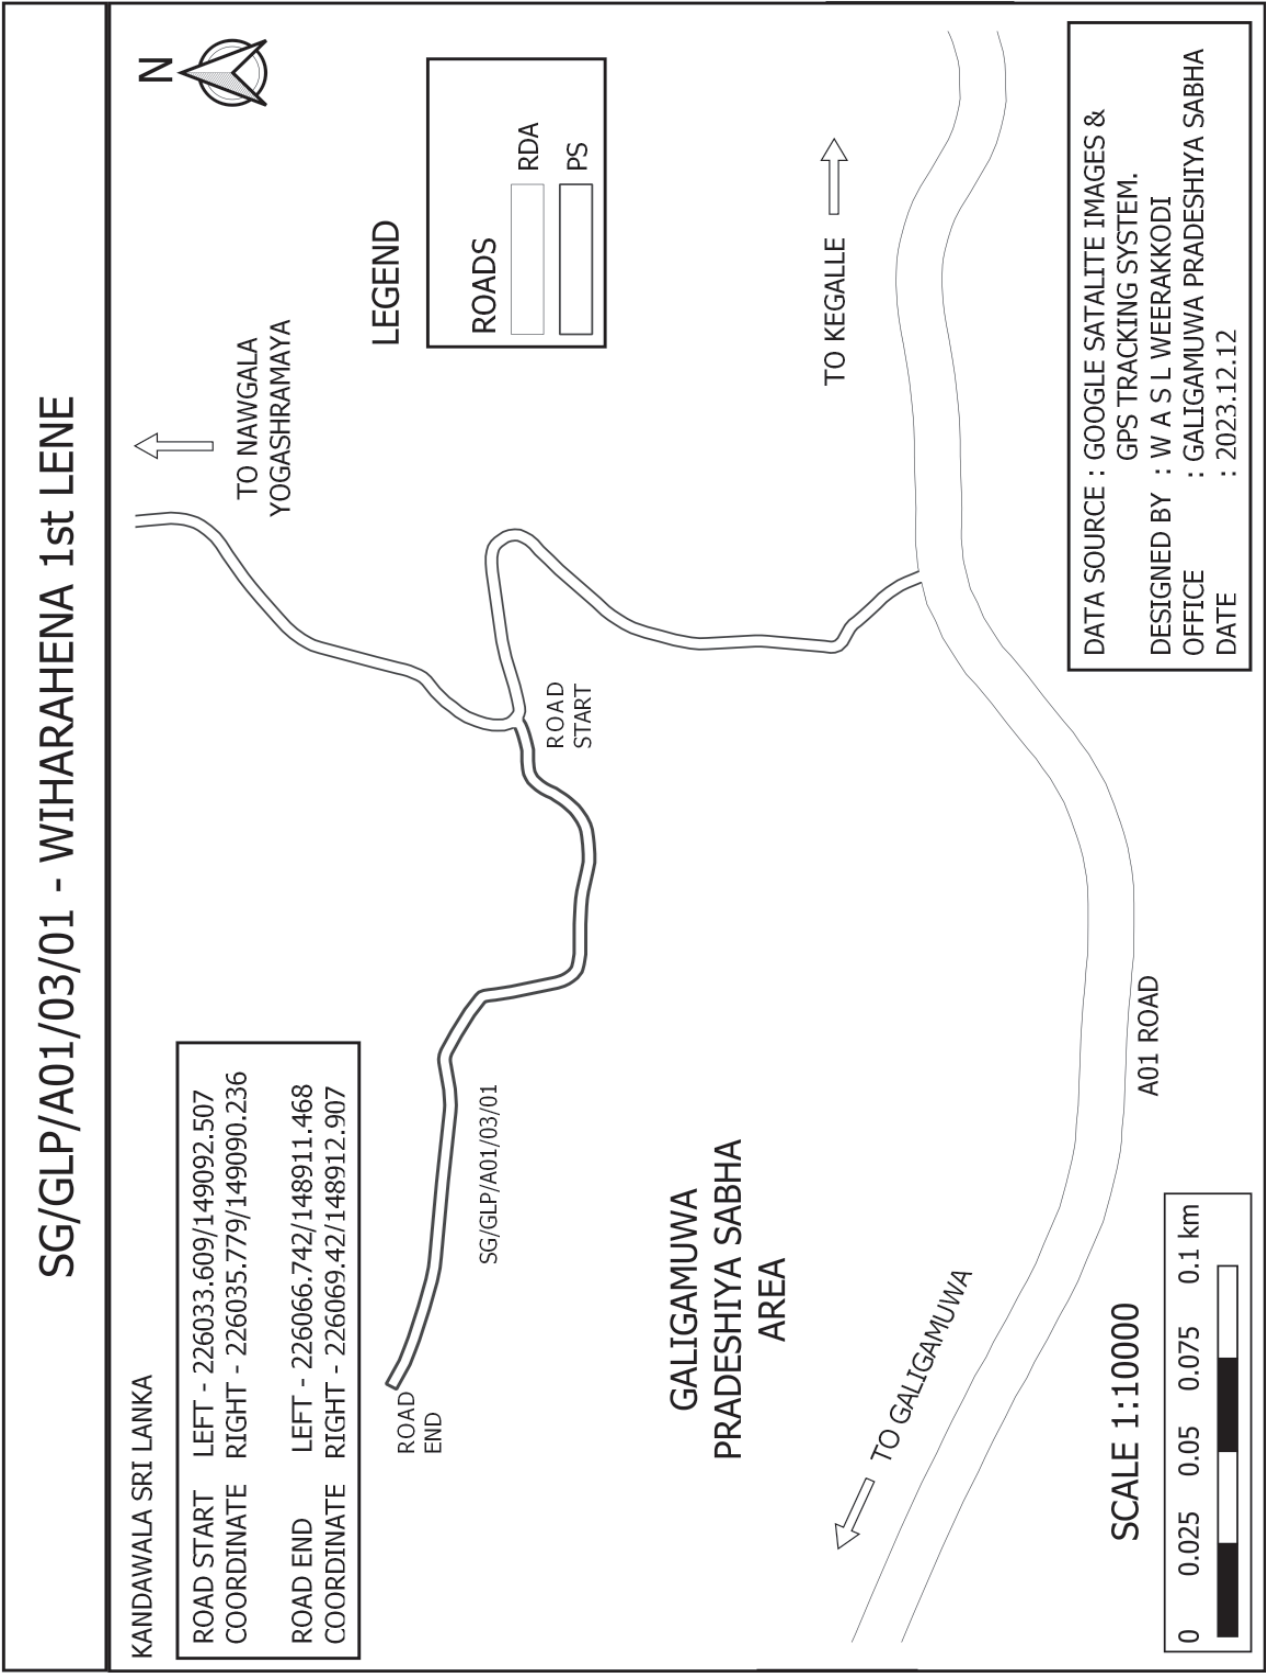


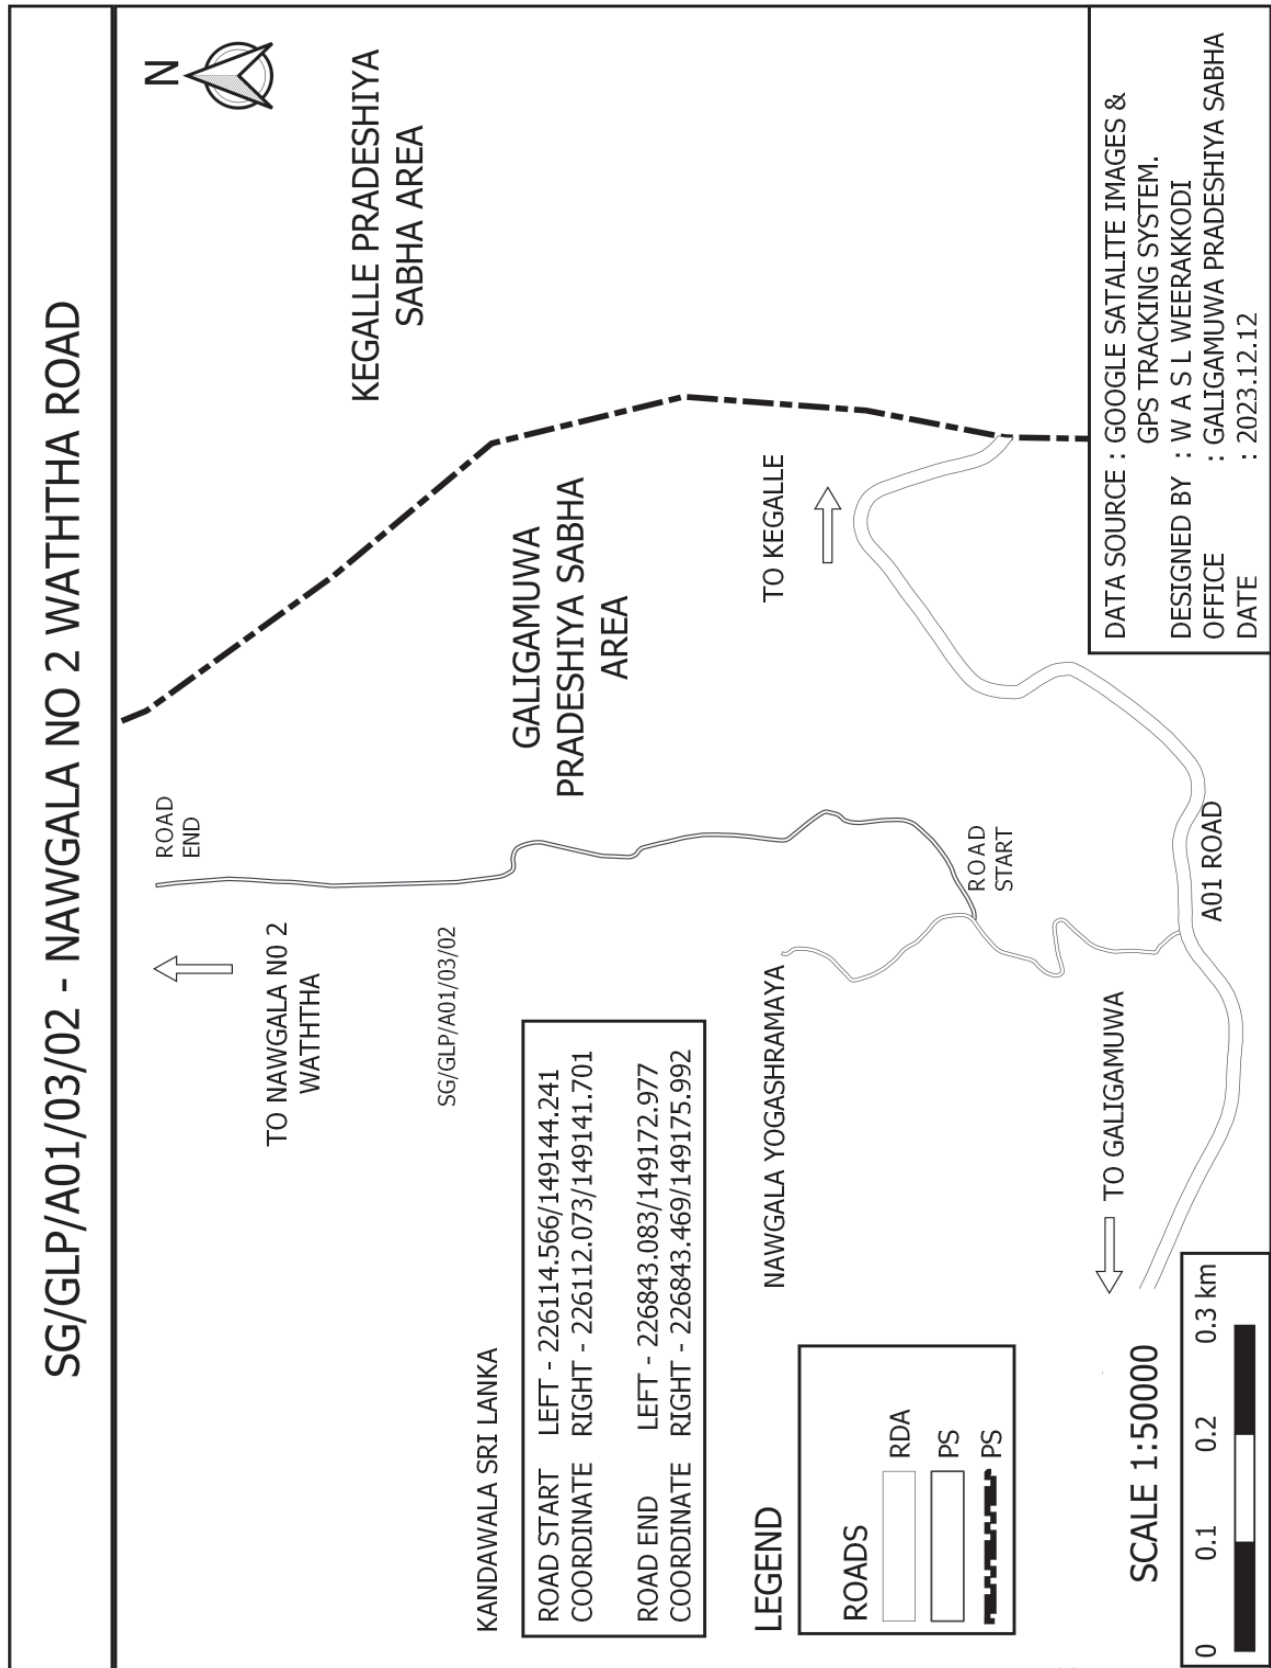


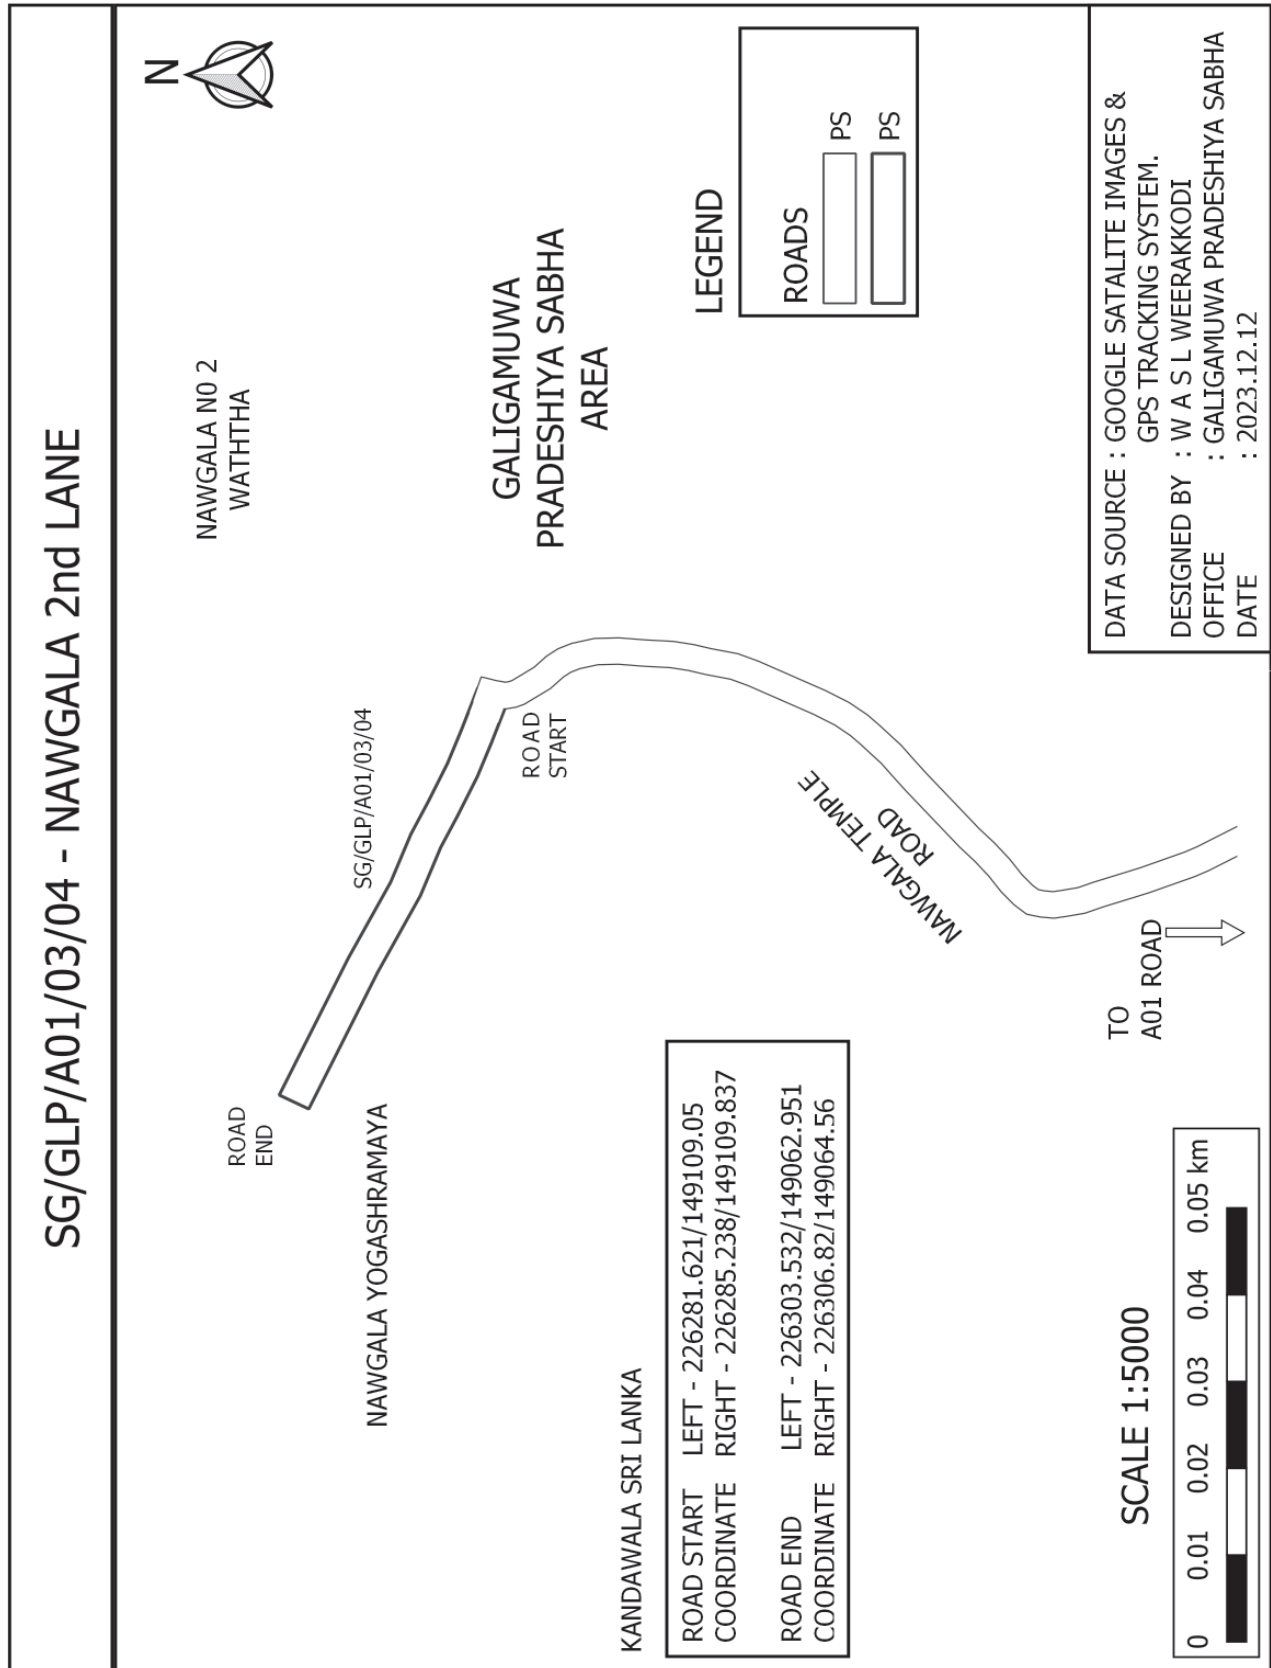


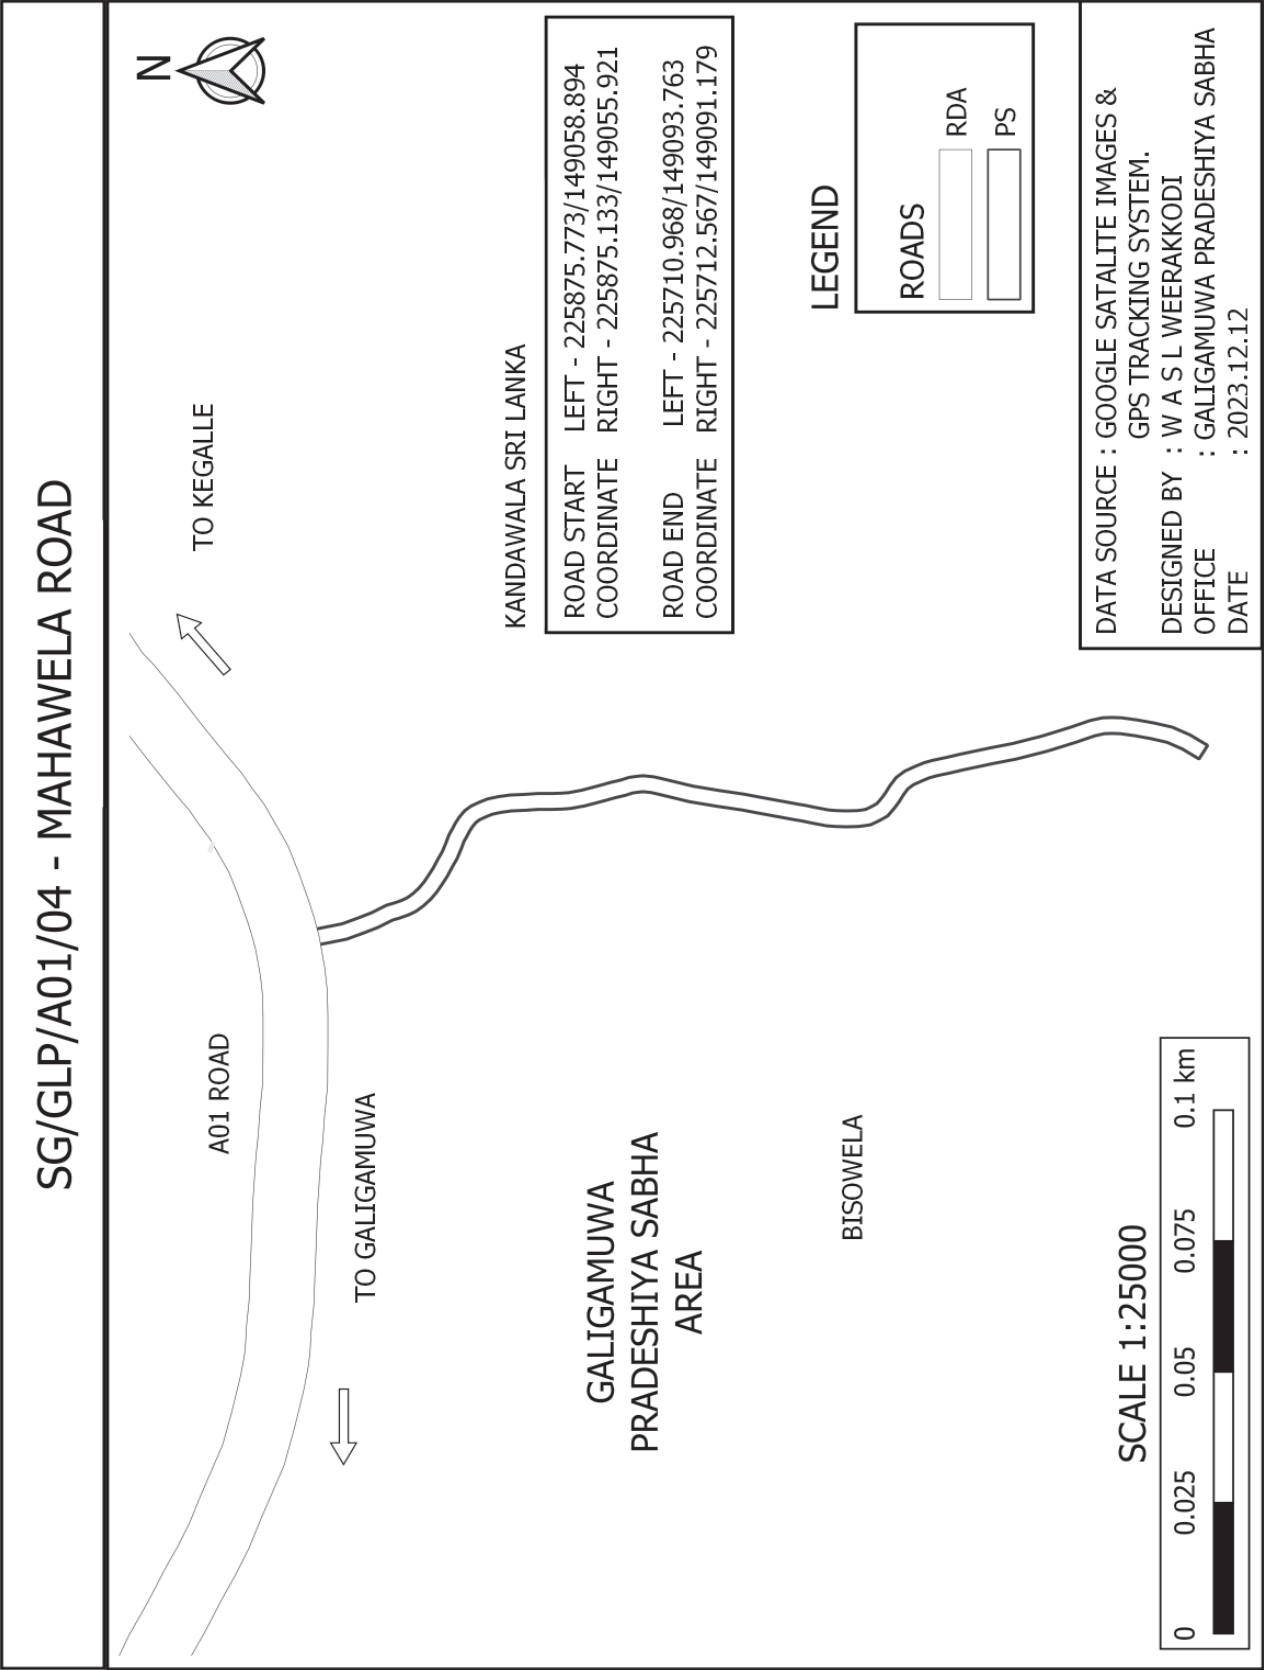


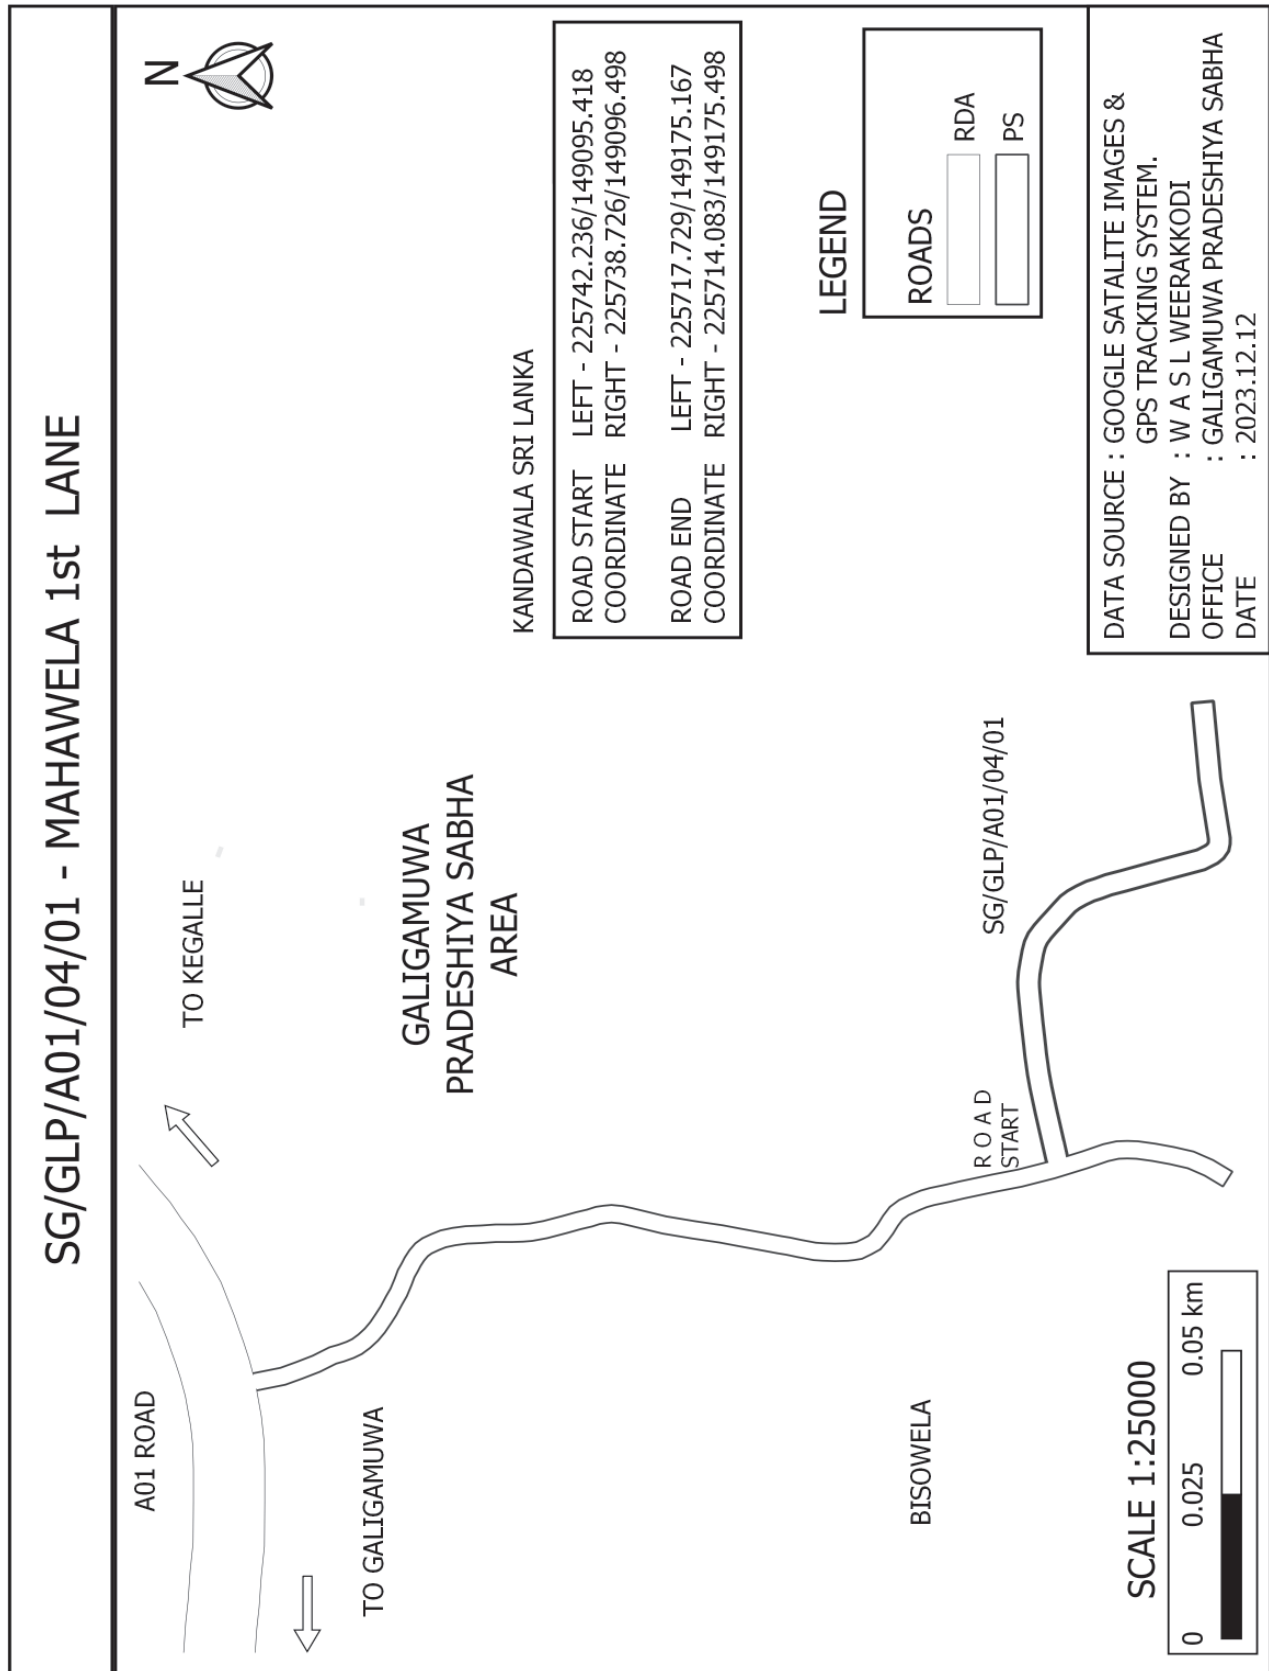


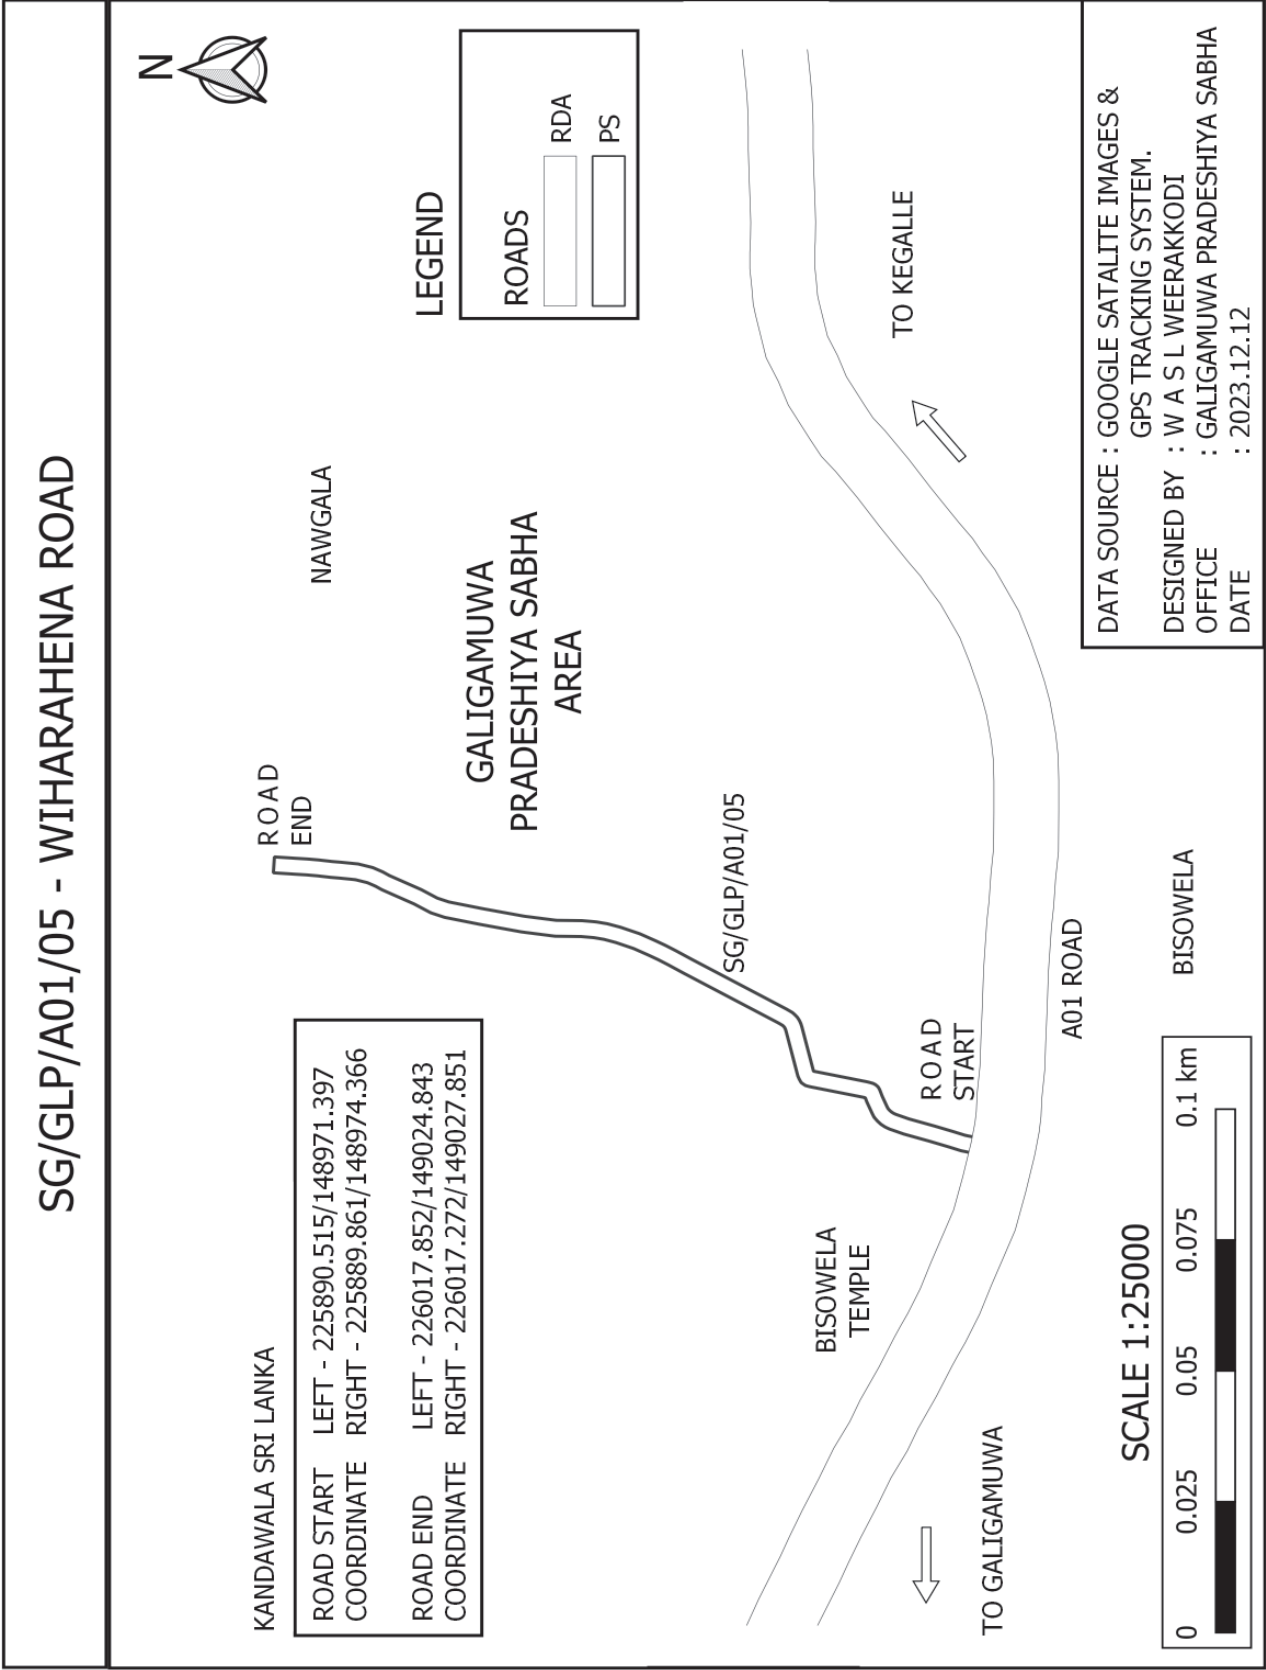

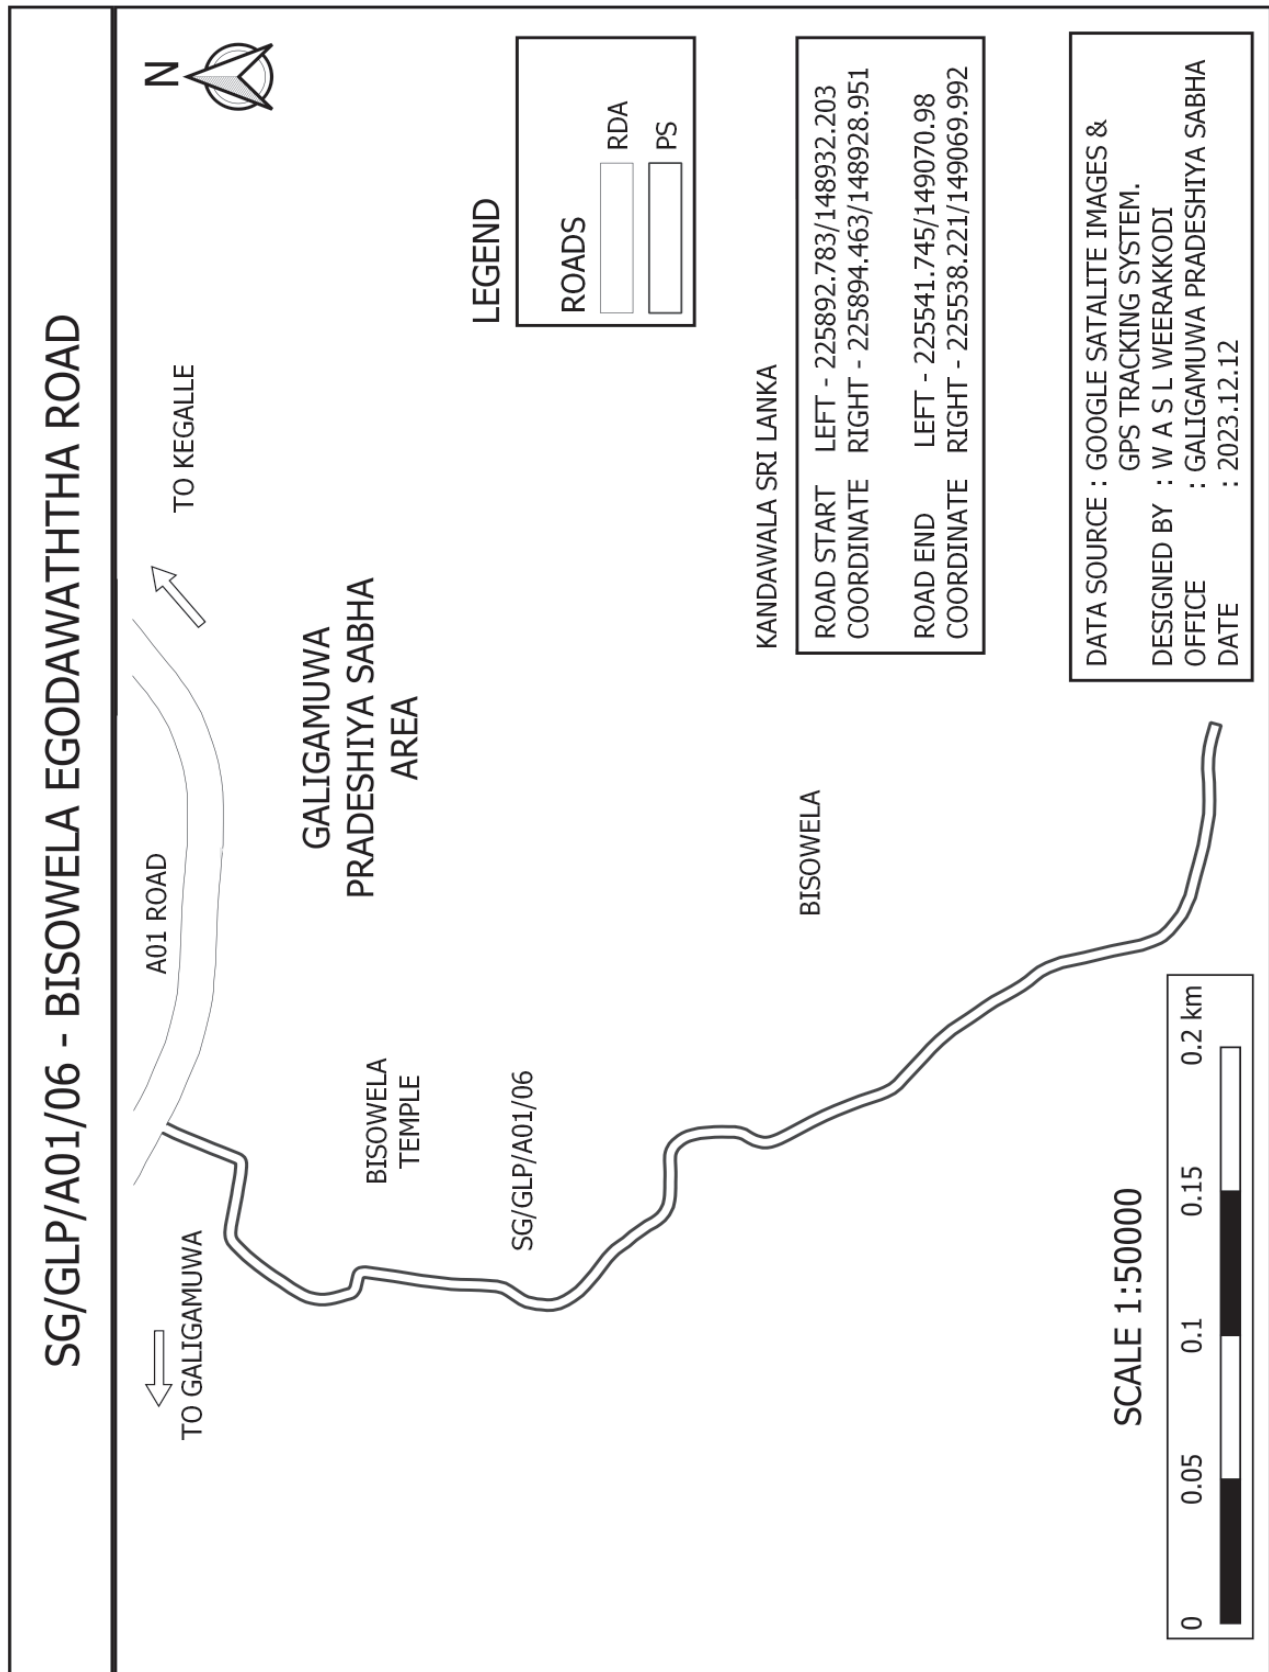

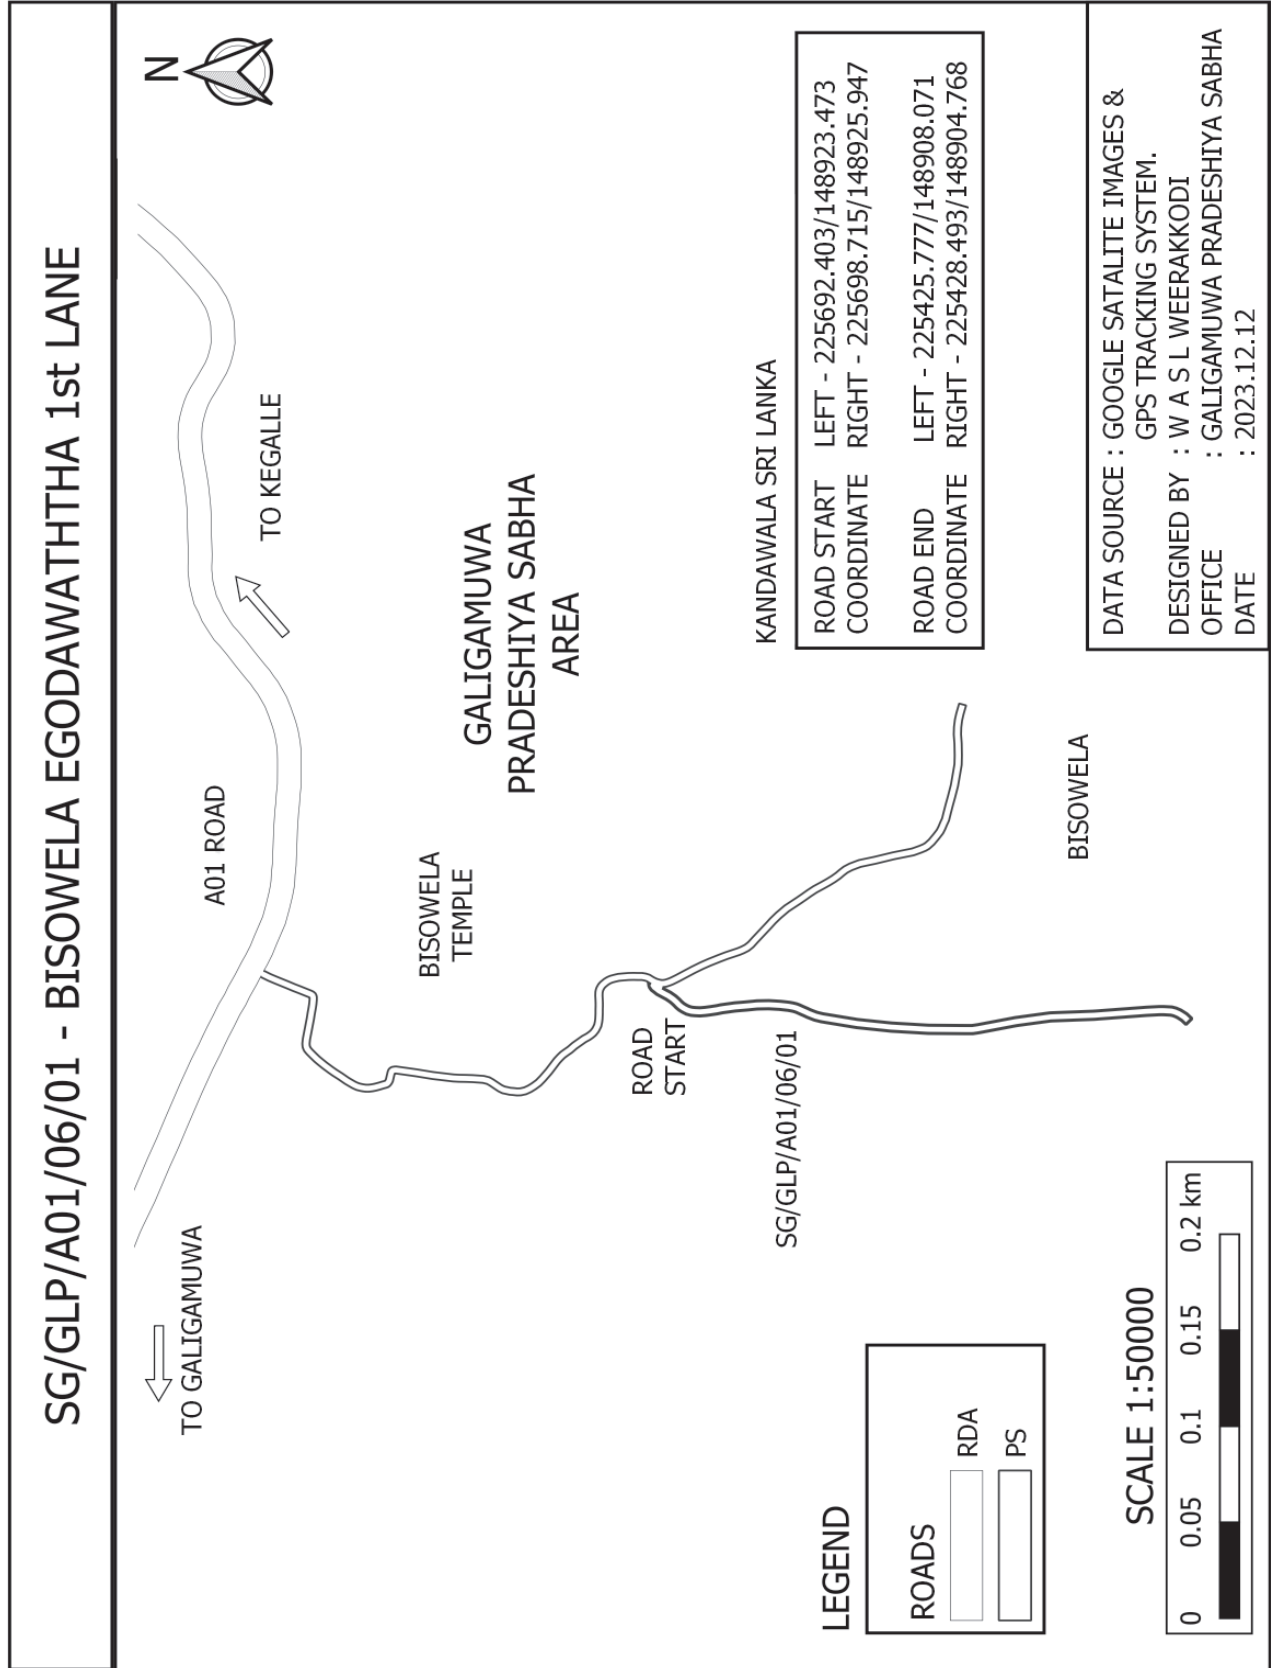

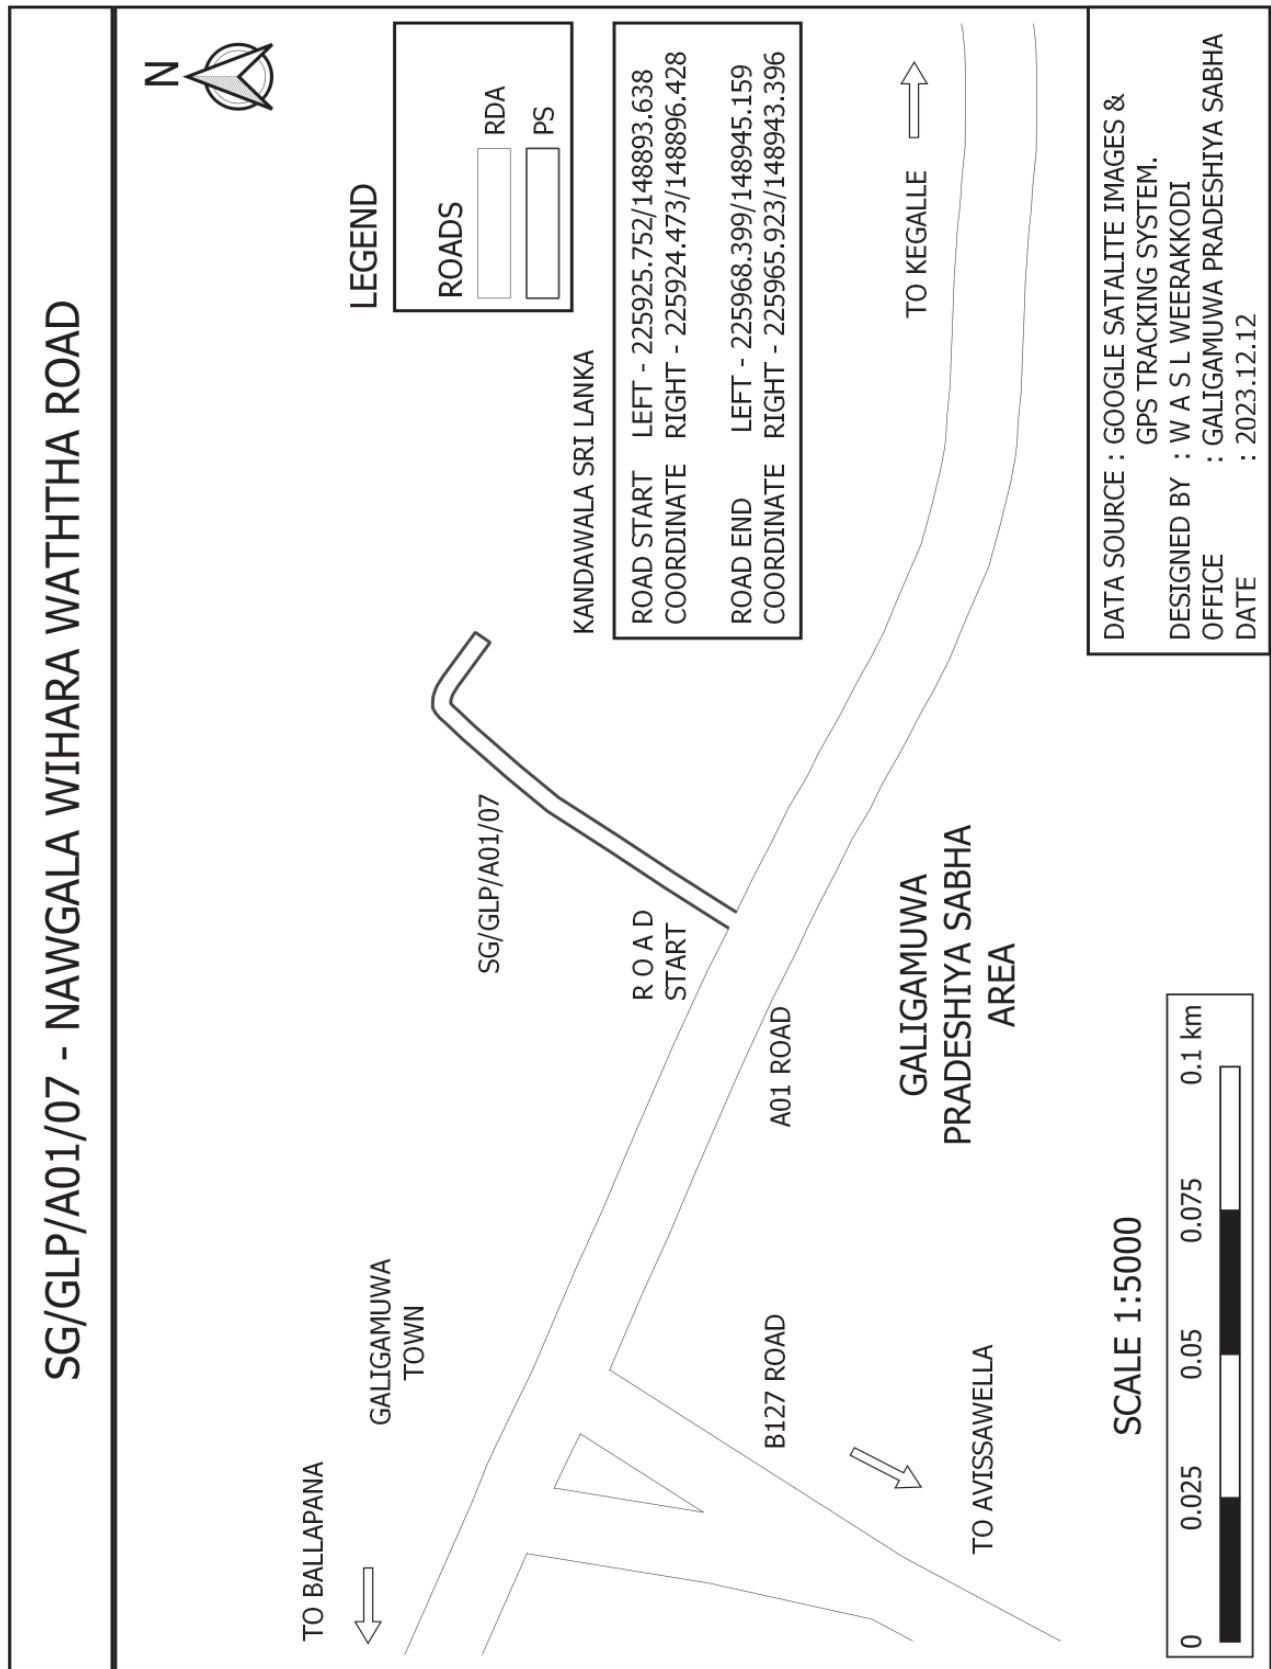

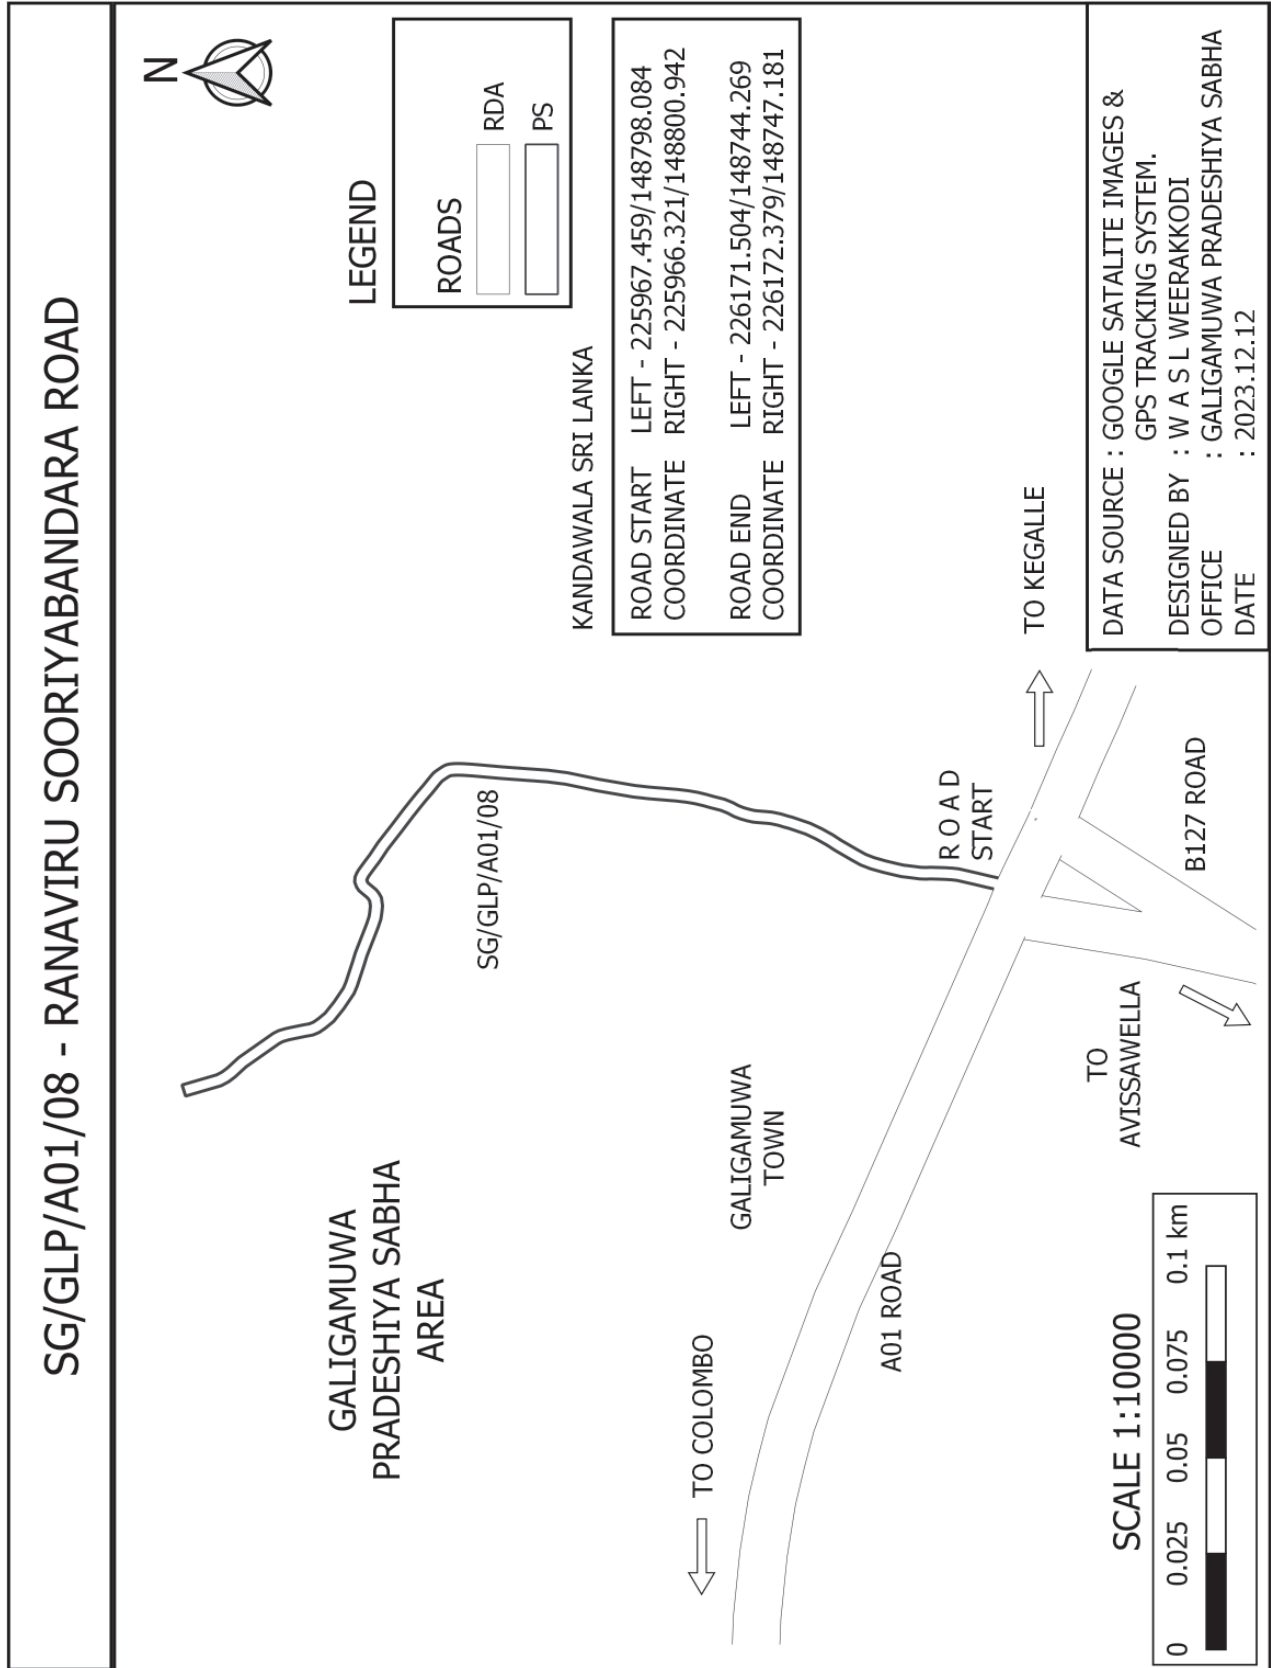



DATA SOURCE : GOOGLE SATALITE IMAGES & GPS TRACKING SYSTEM.


DESIGNED BY : W A S L WEERAKKODI


OFFICE : GALIGAMUWA PRADESHIYA SABHA


DATE : 2023.12.12

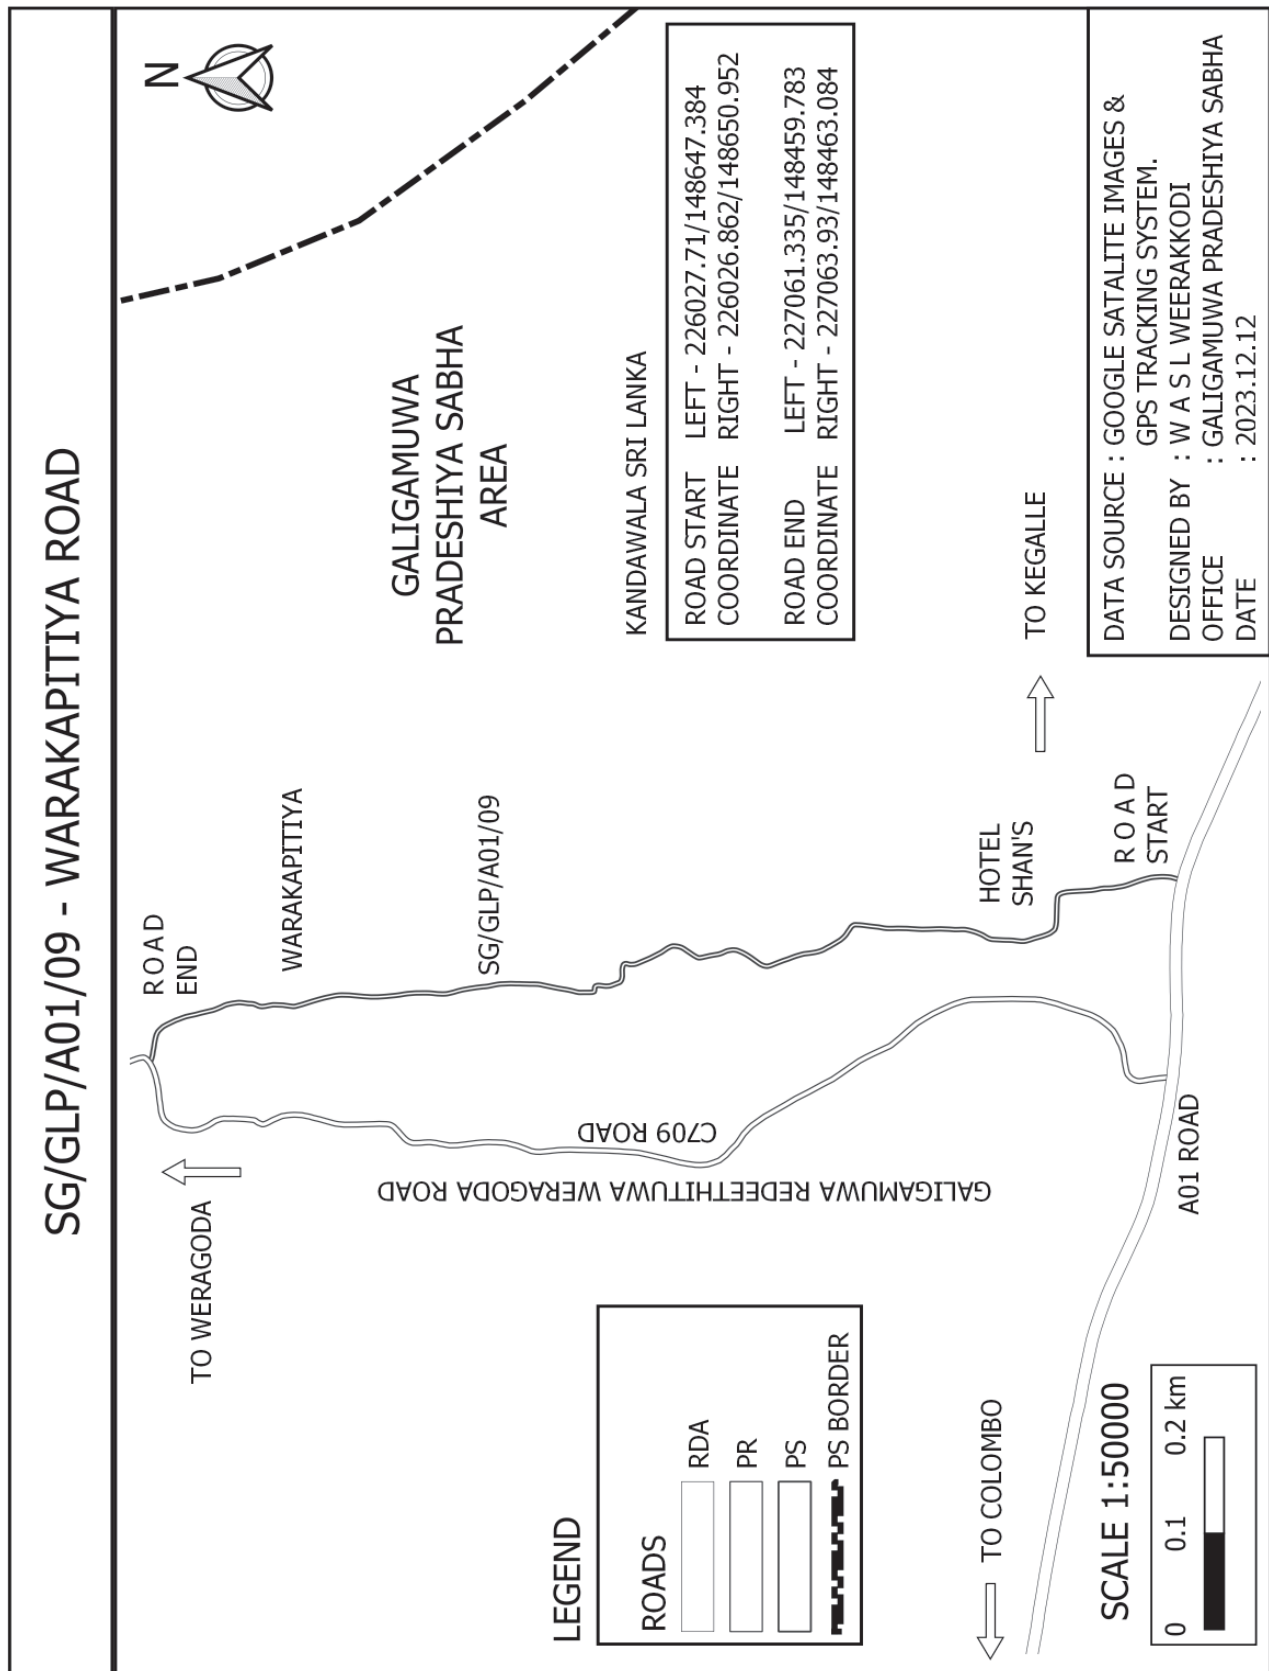


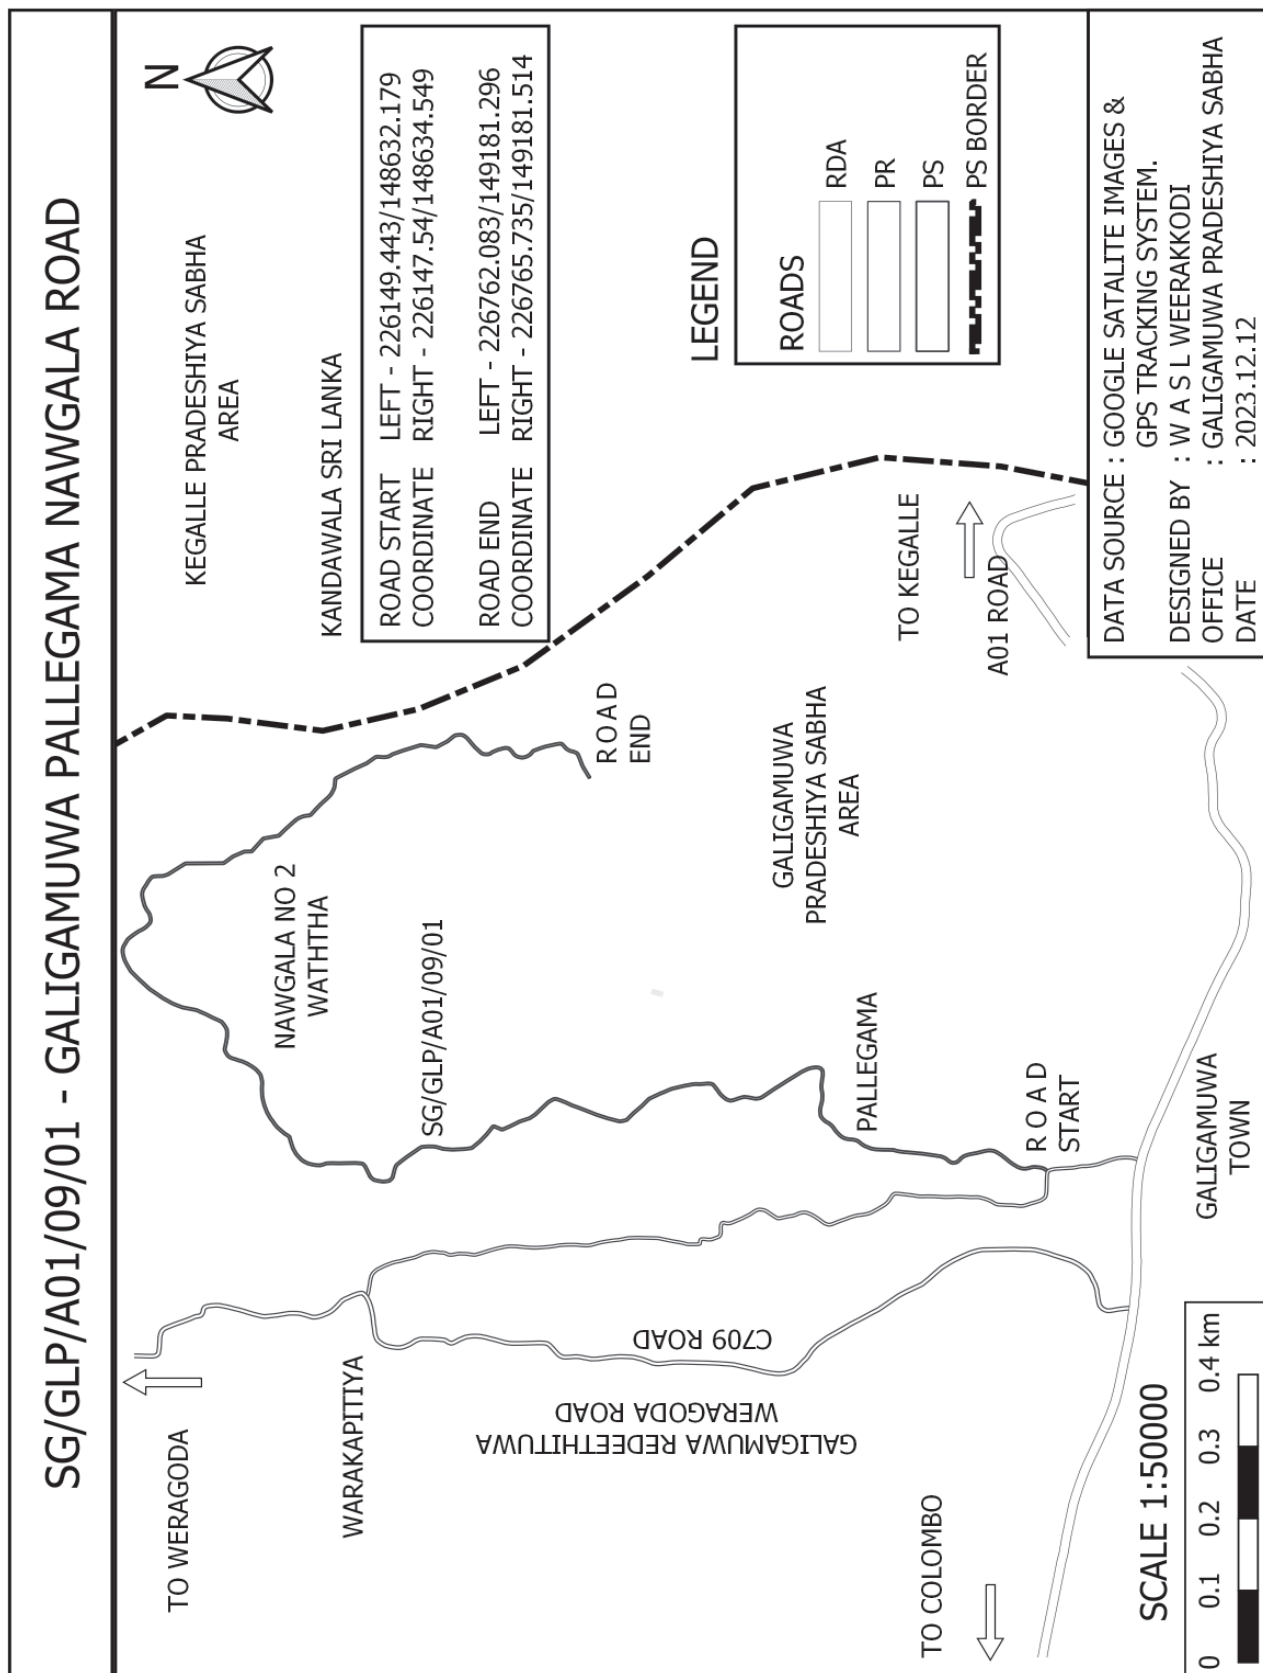

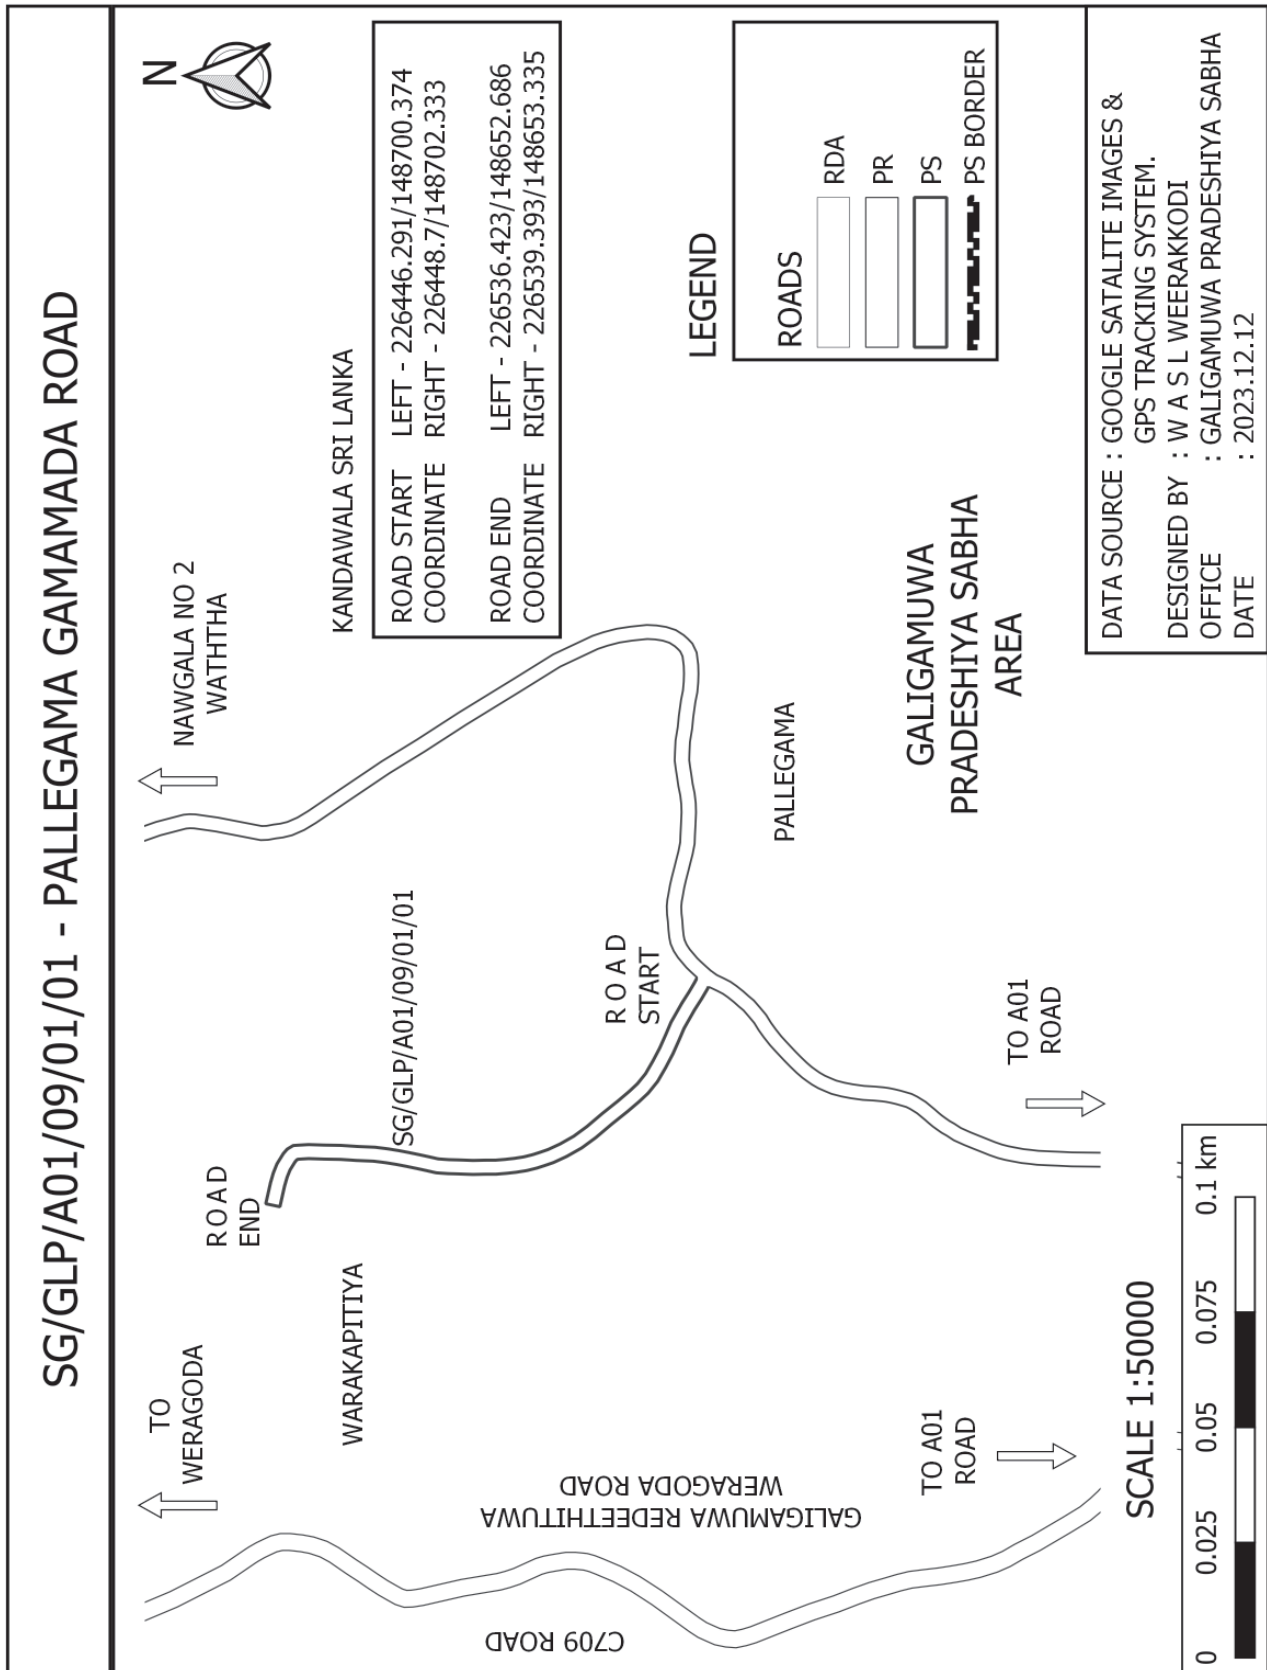


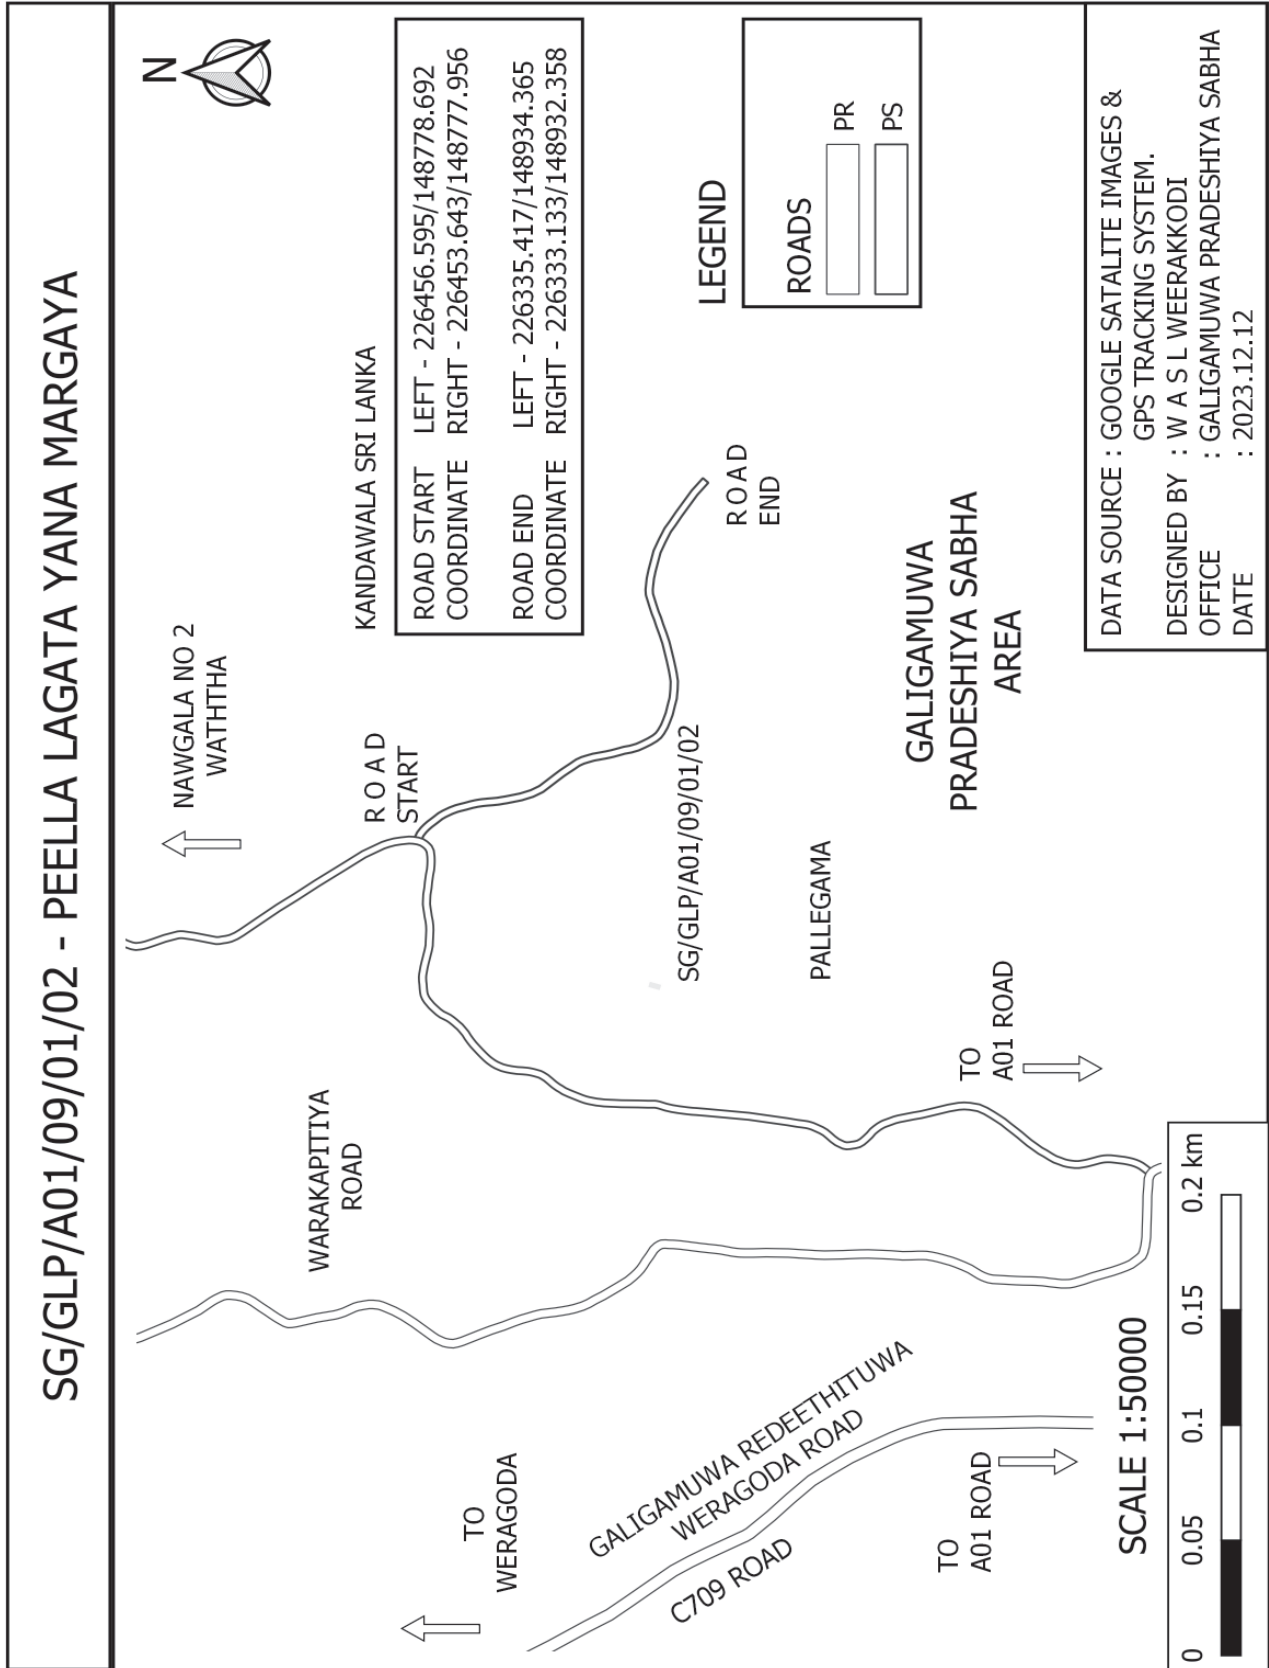


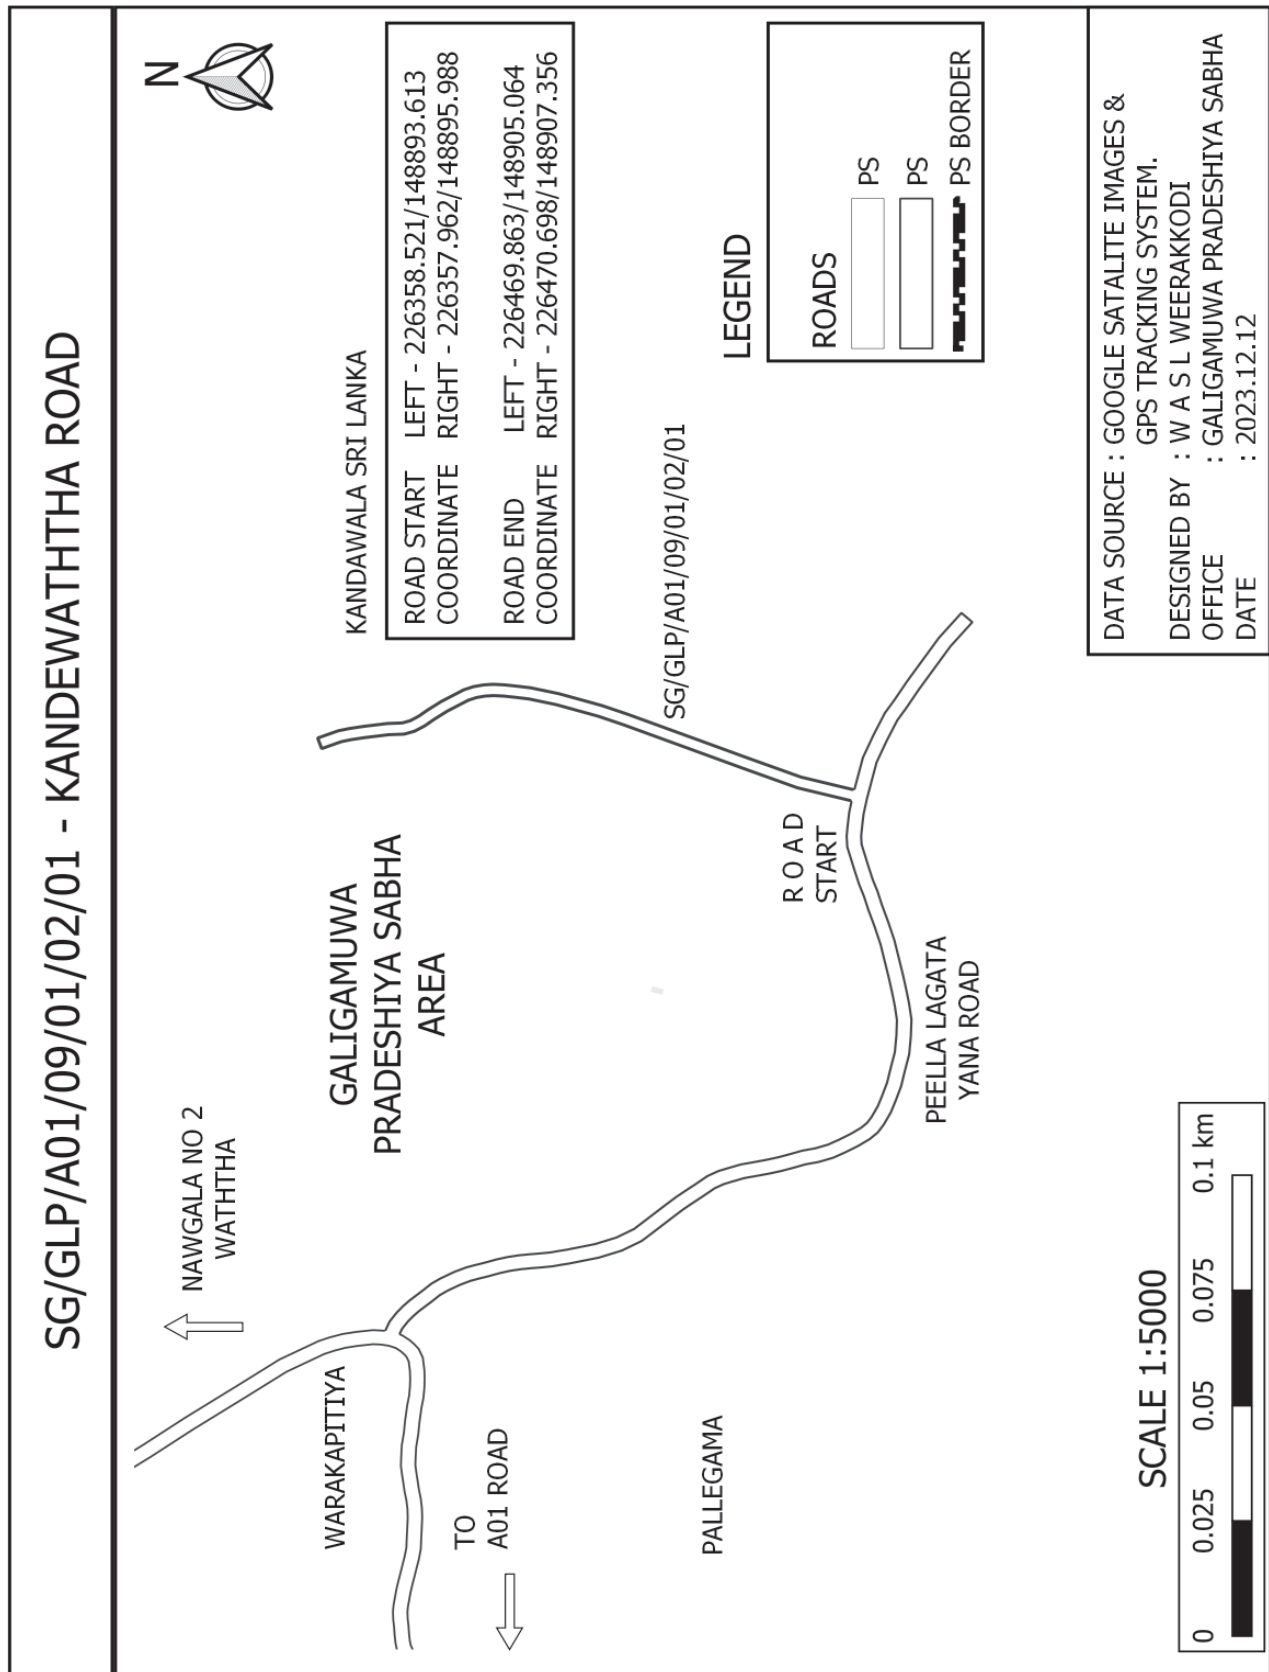


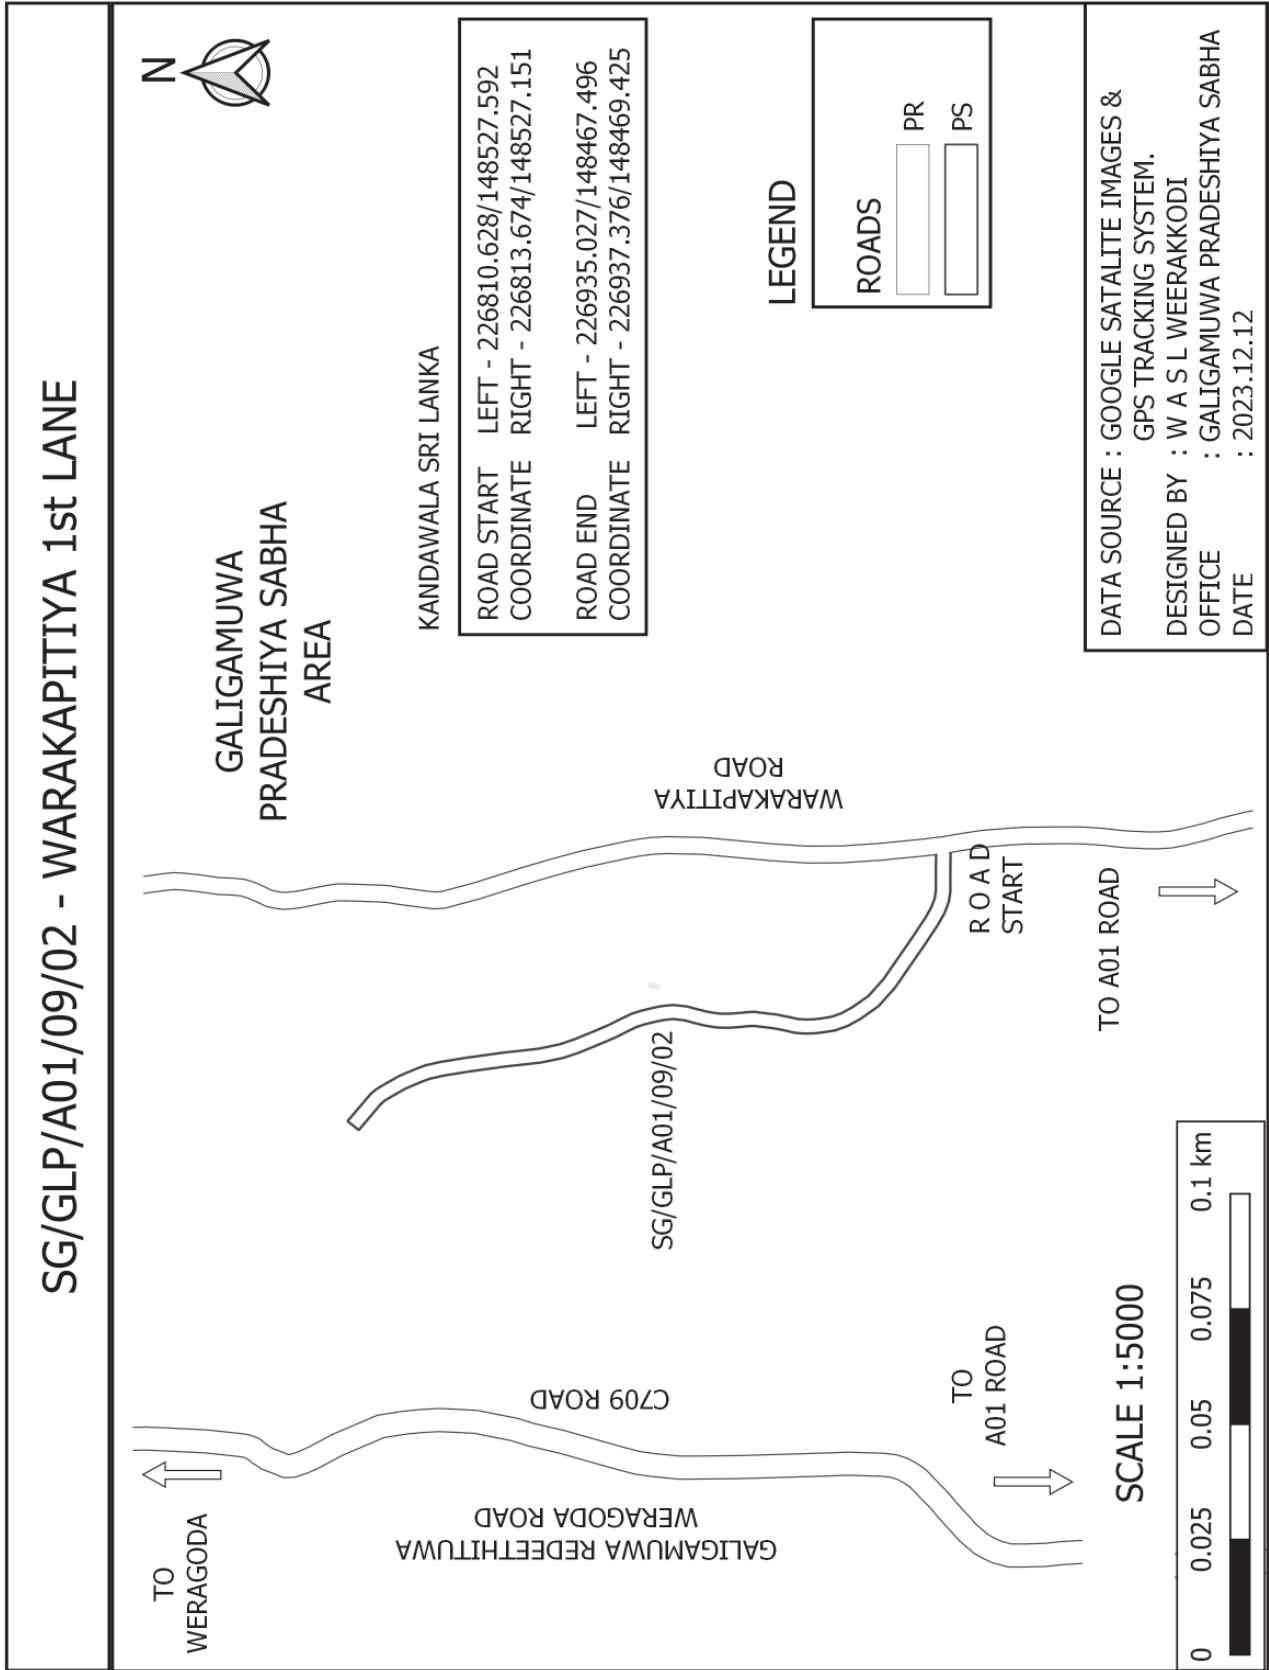





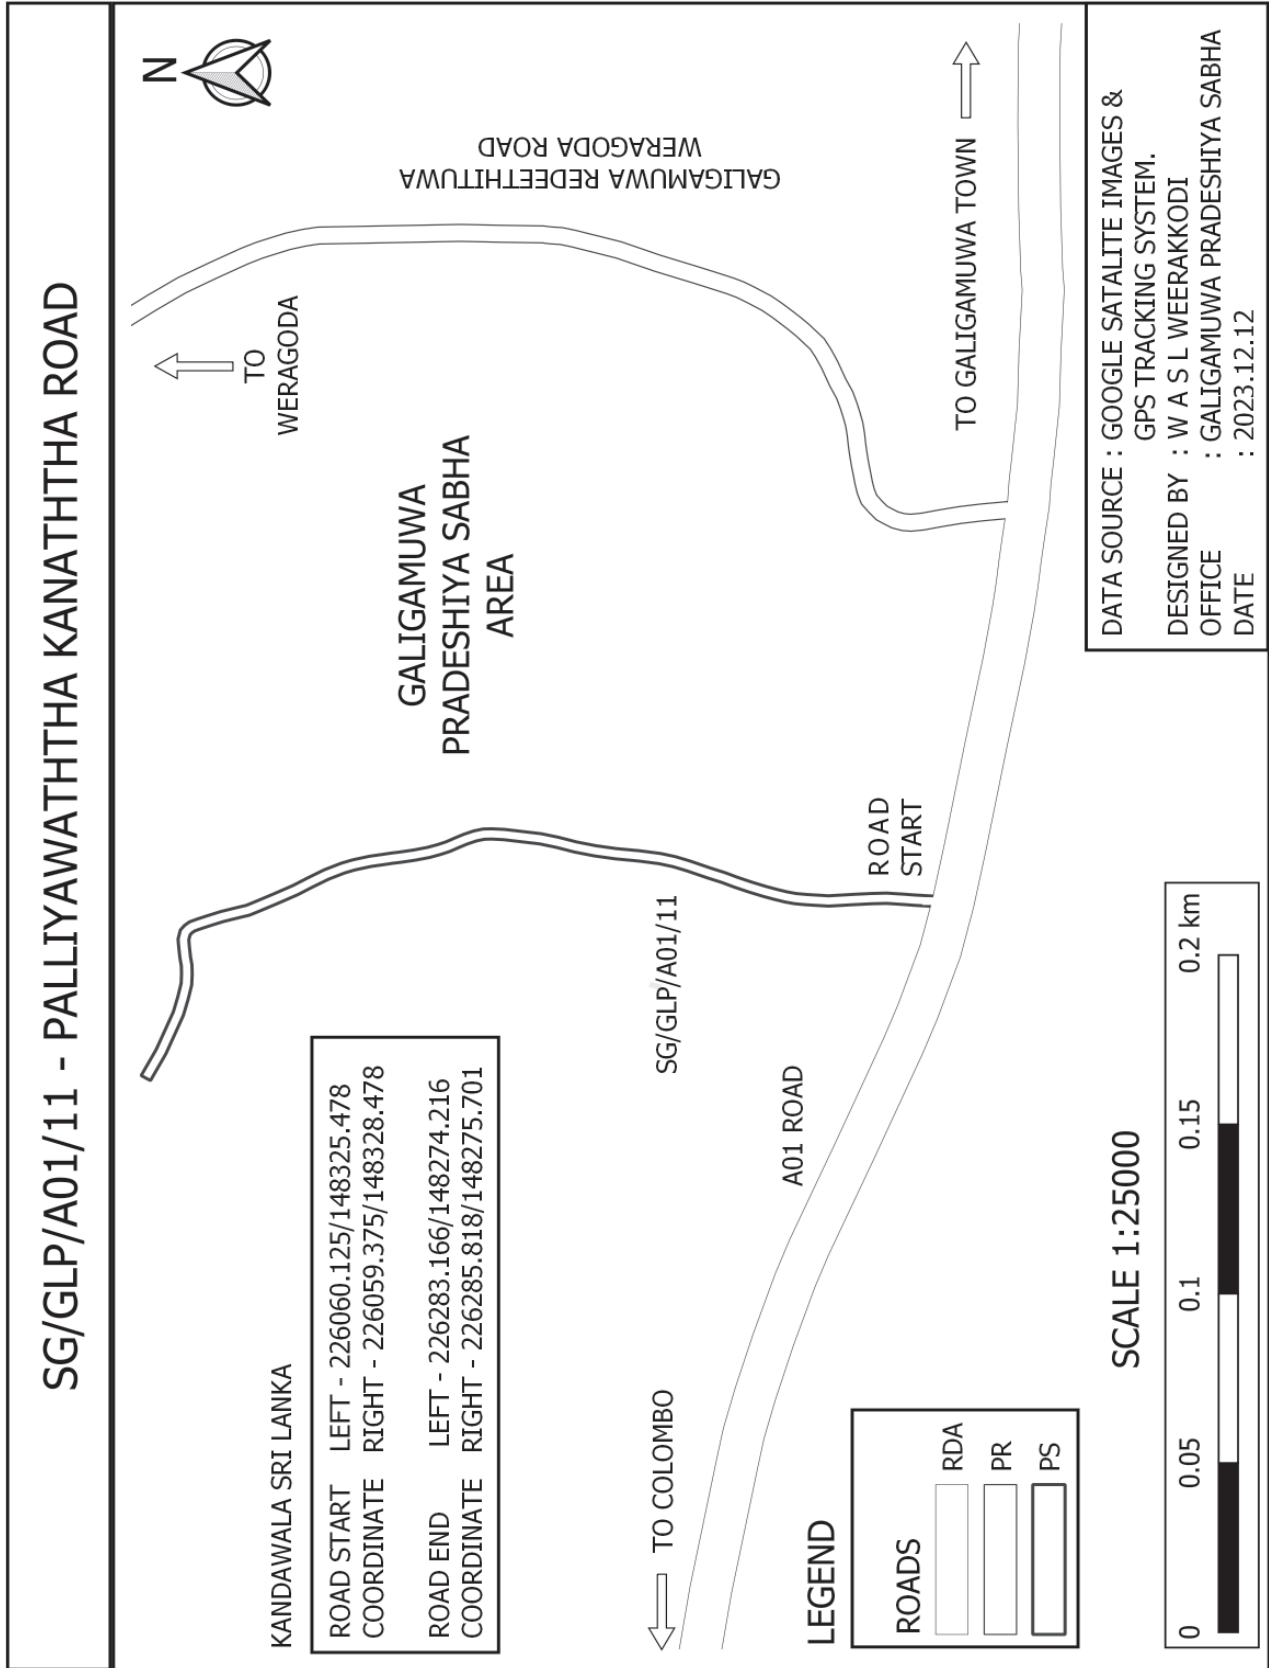


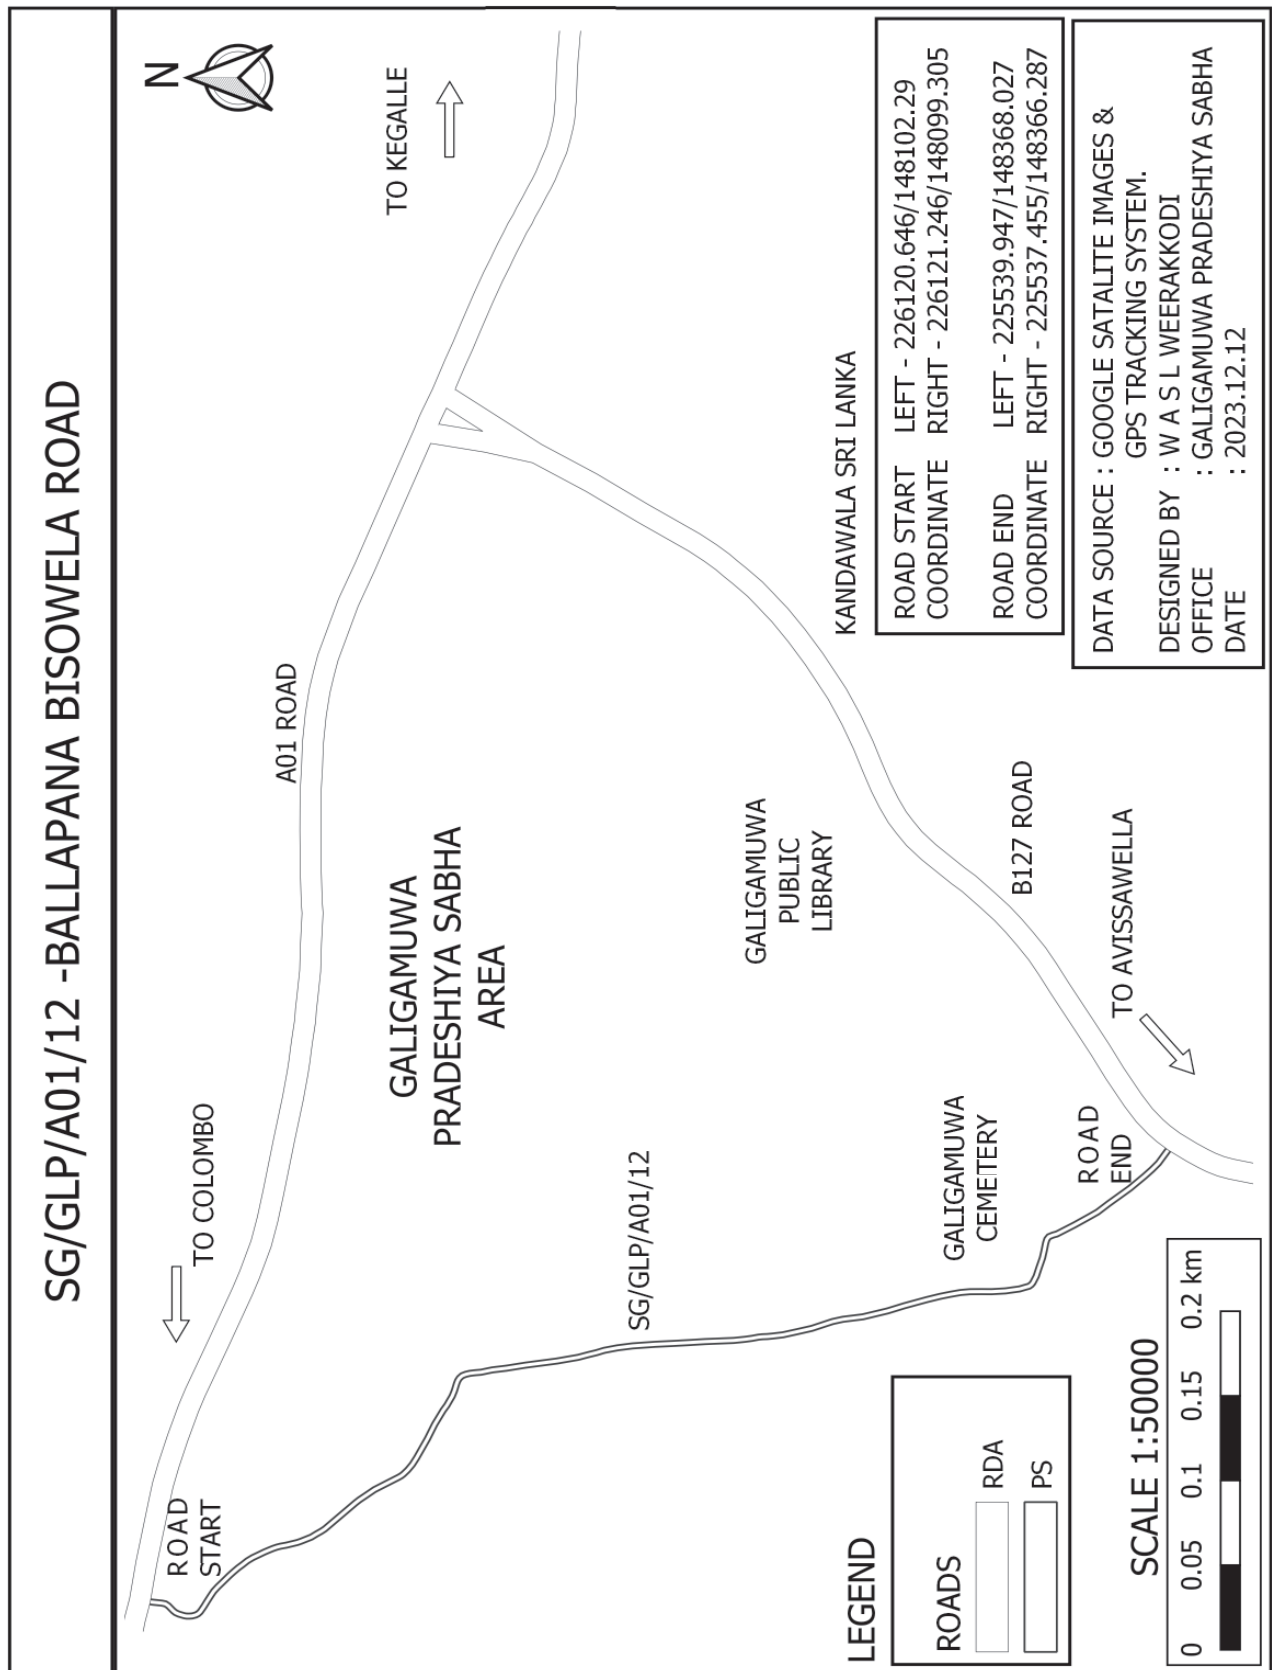


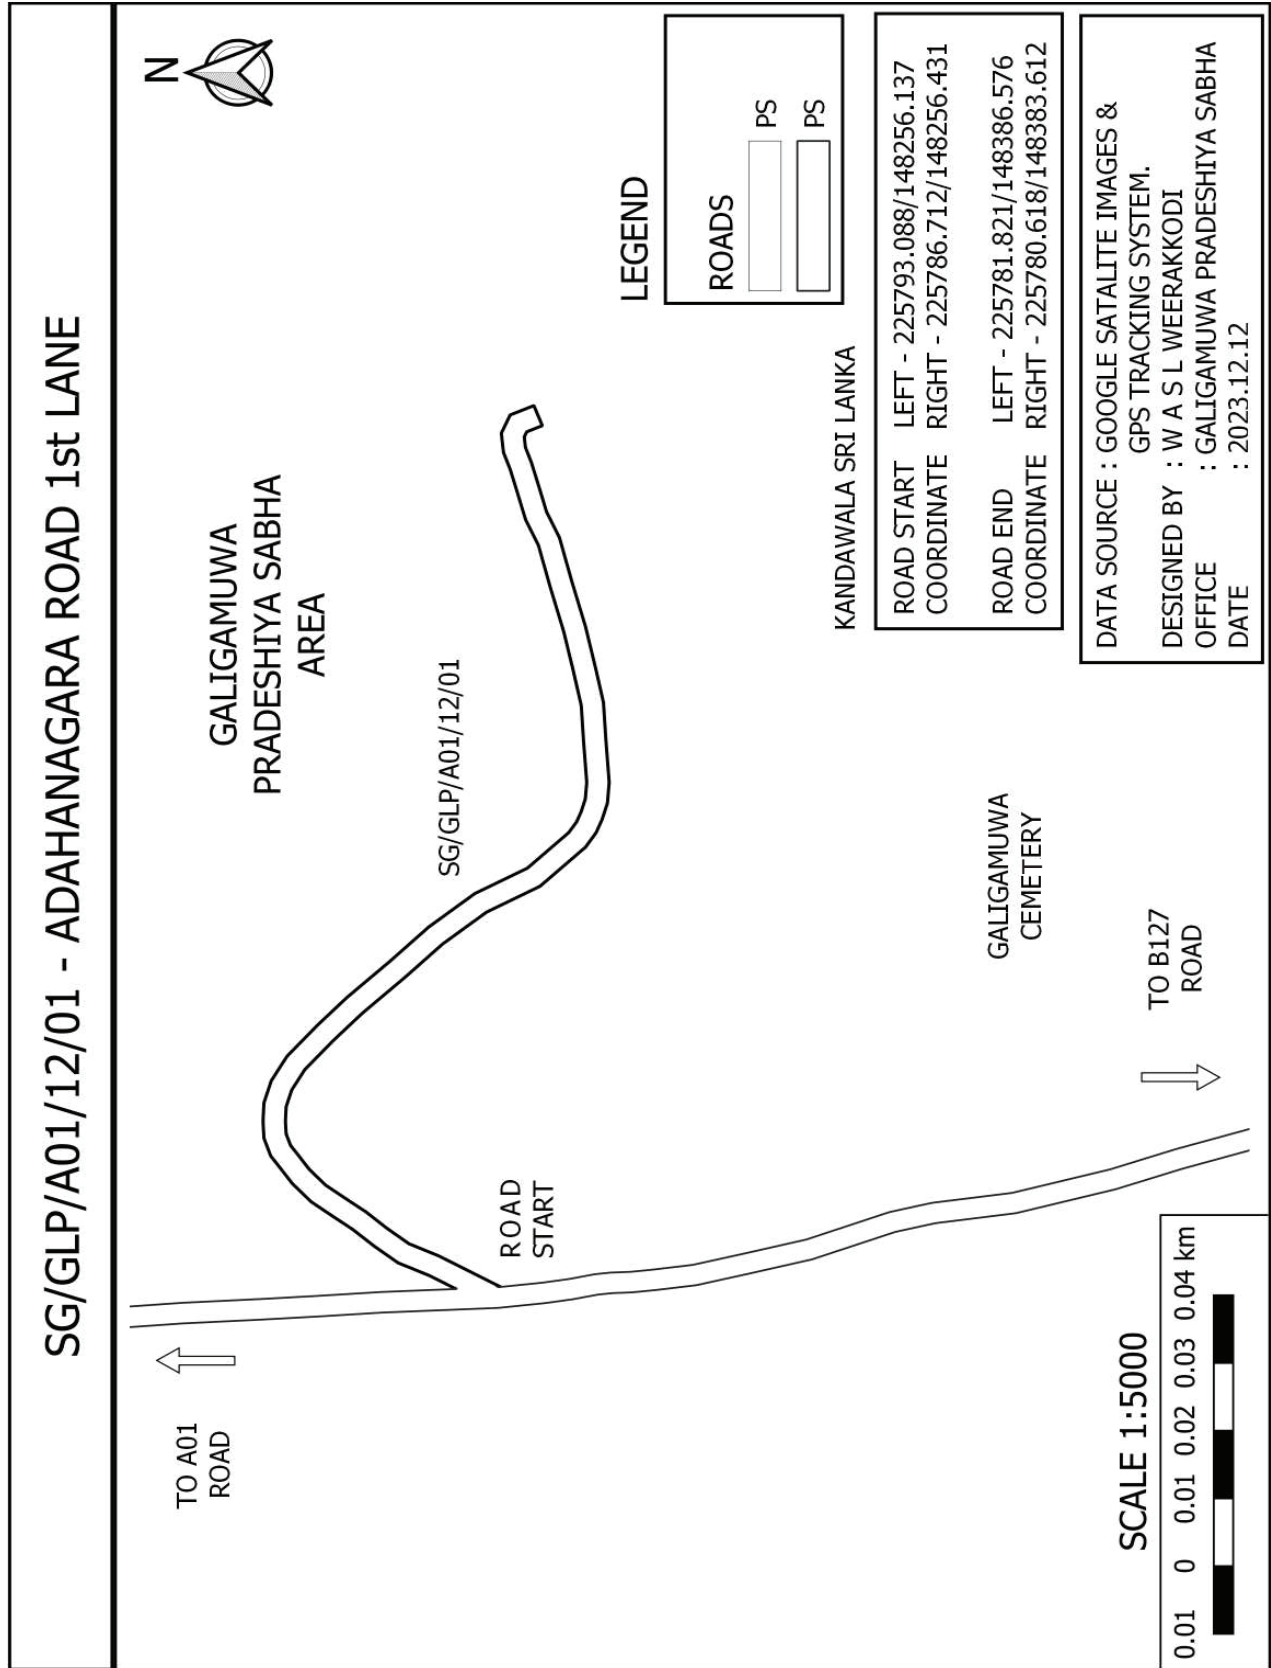


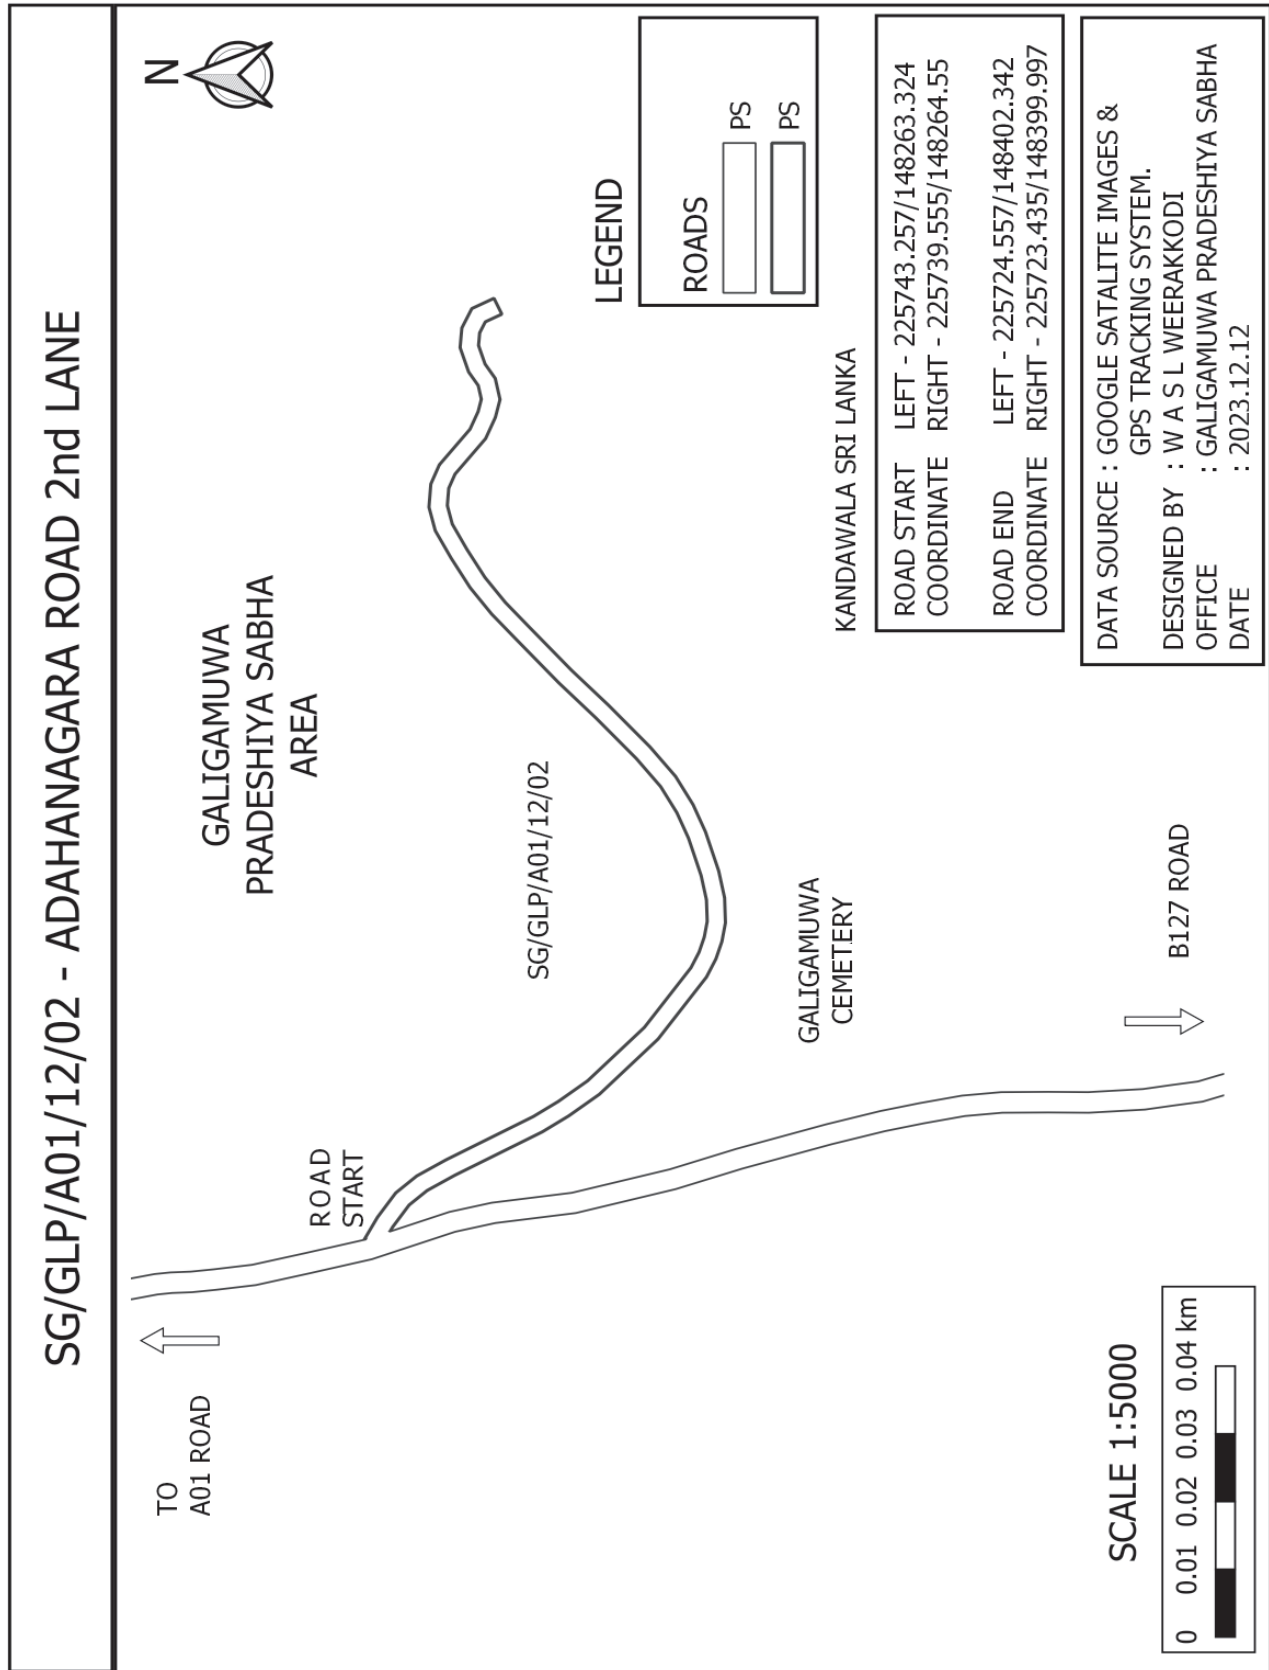


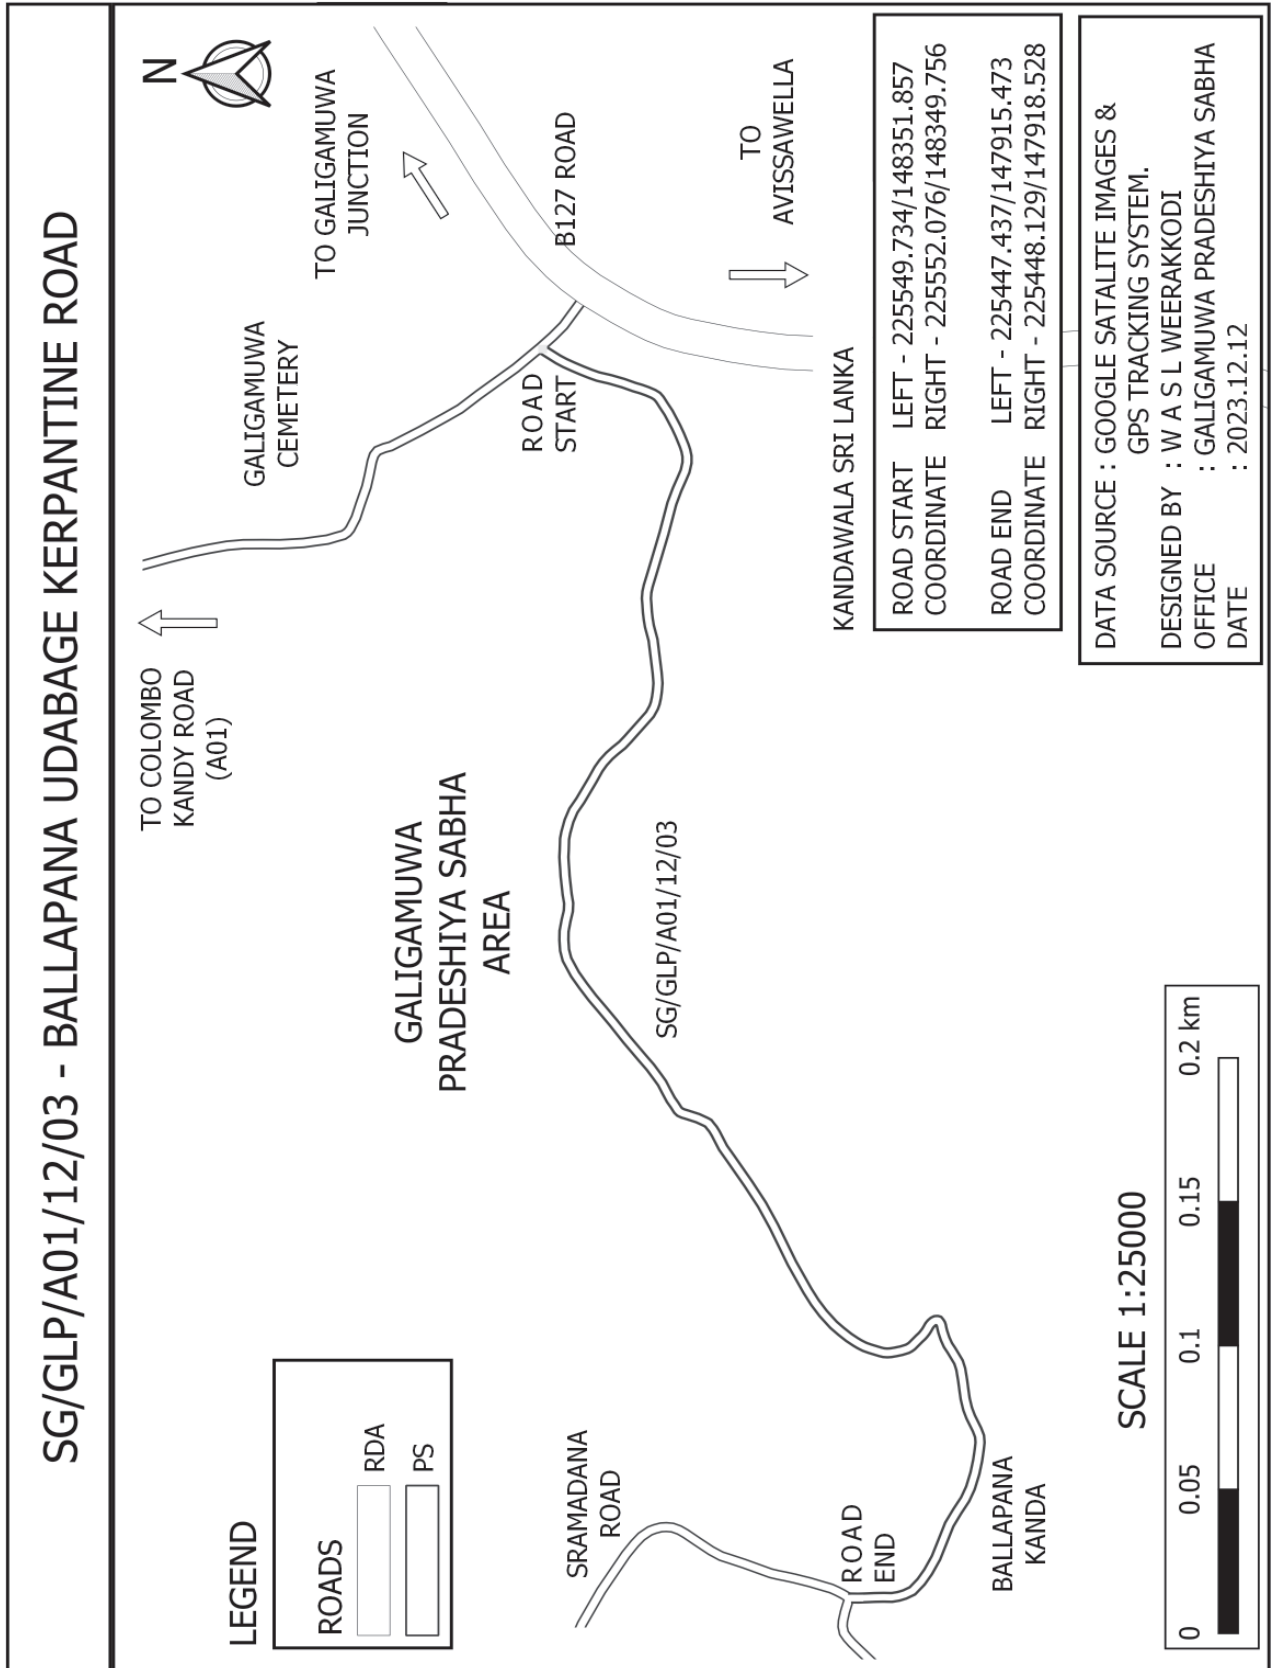


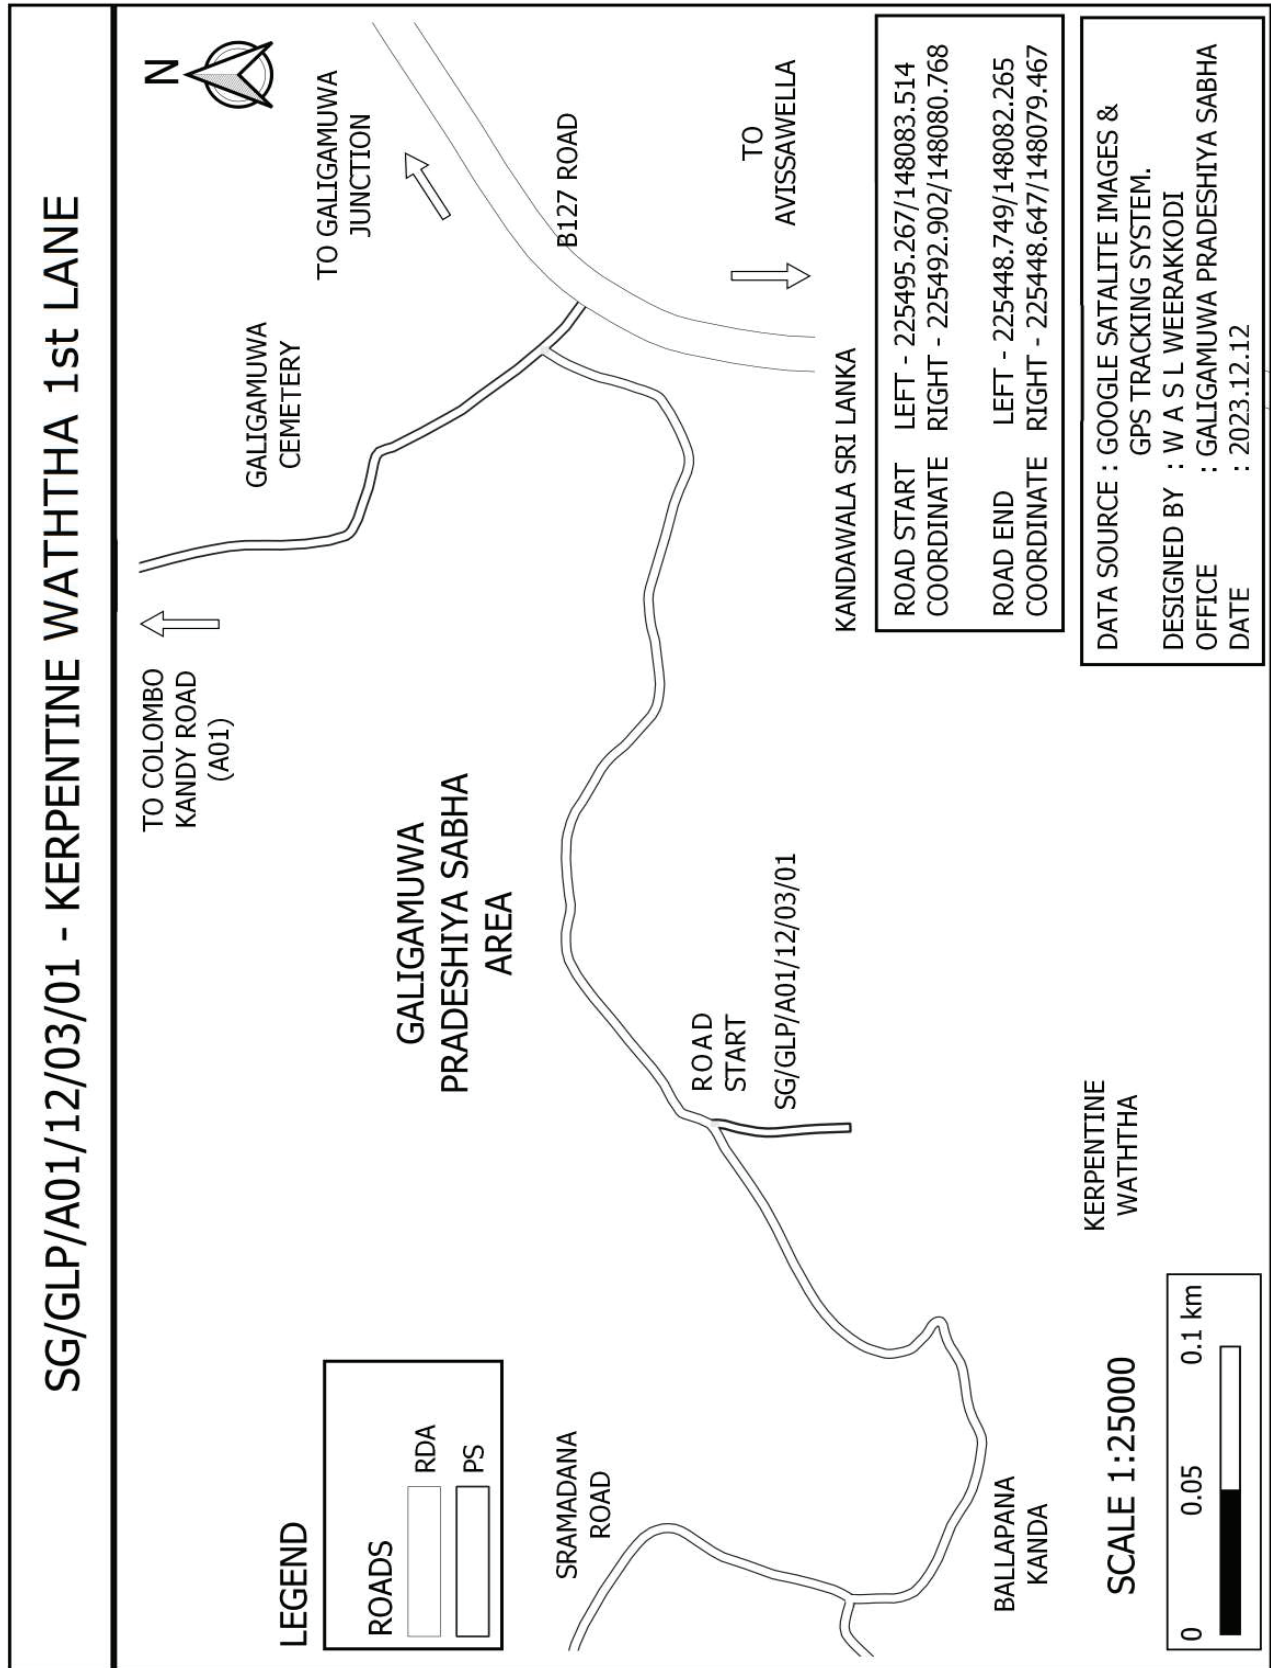


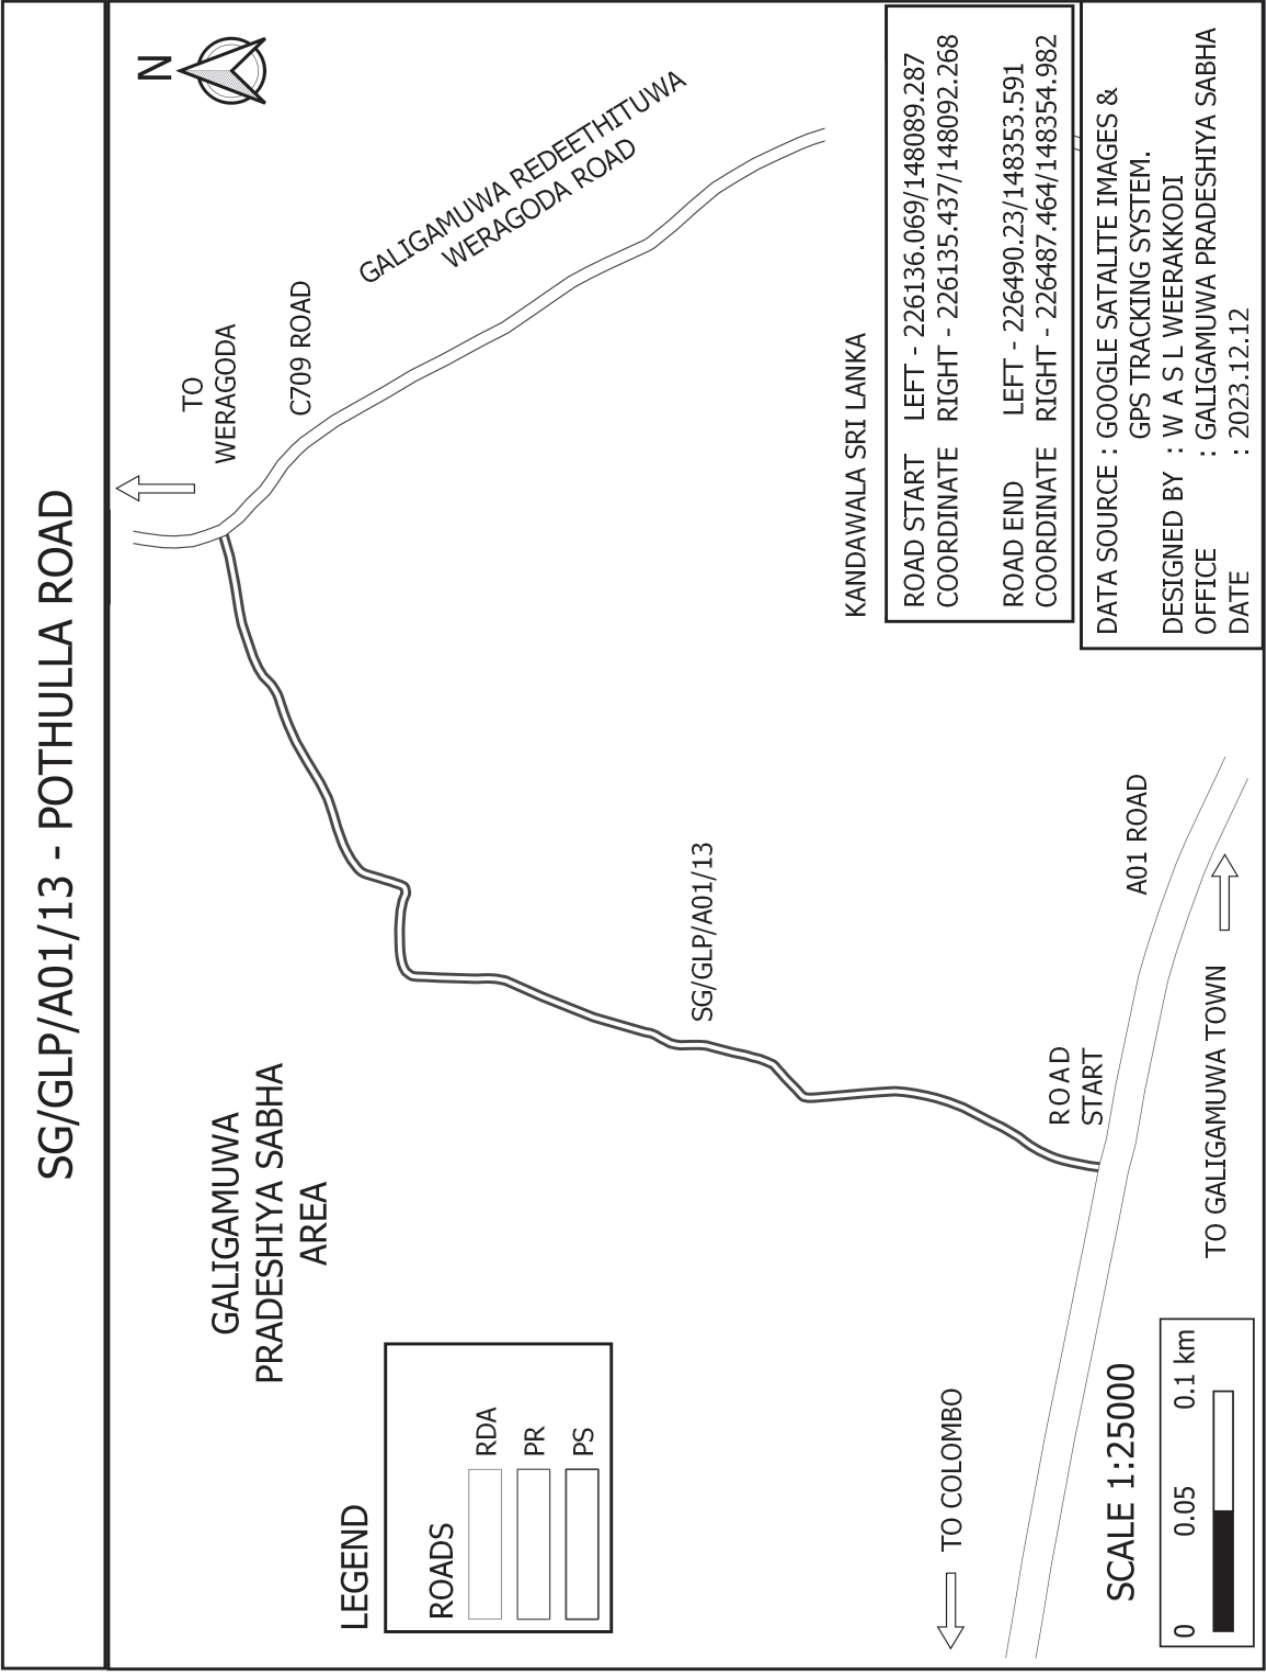


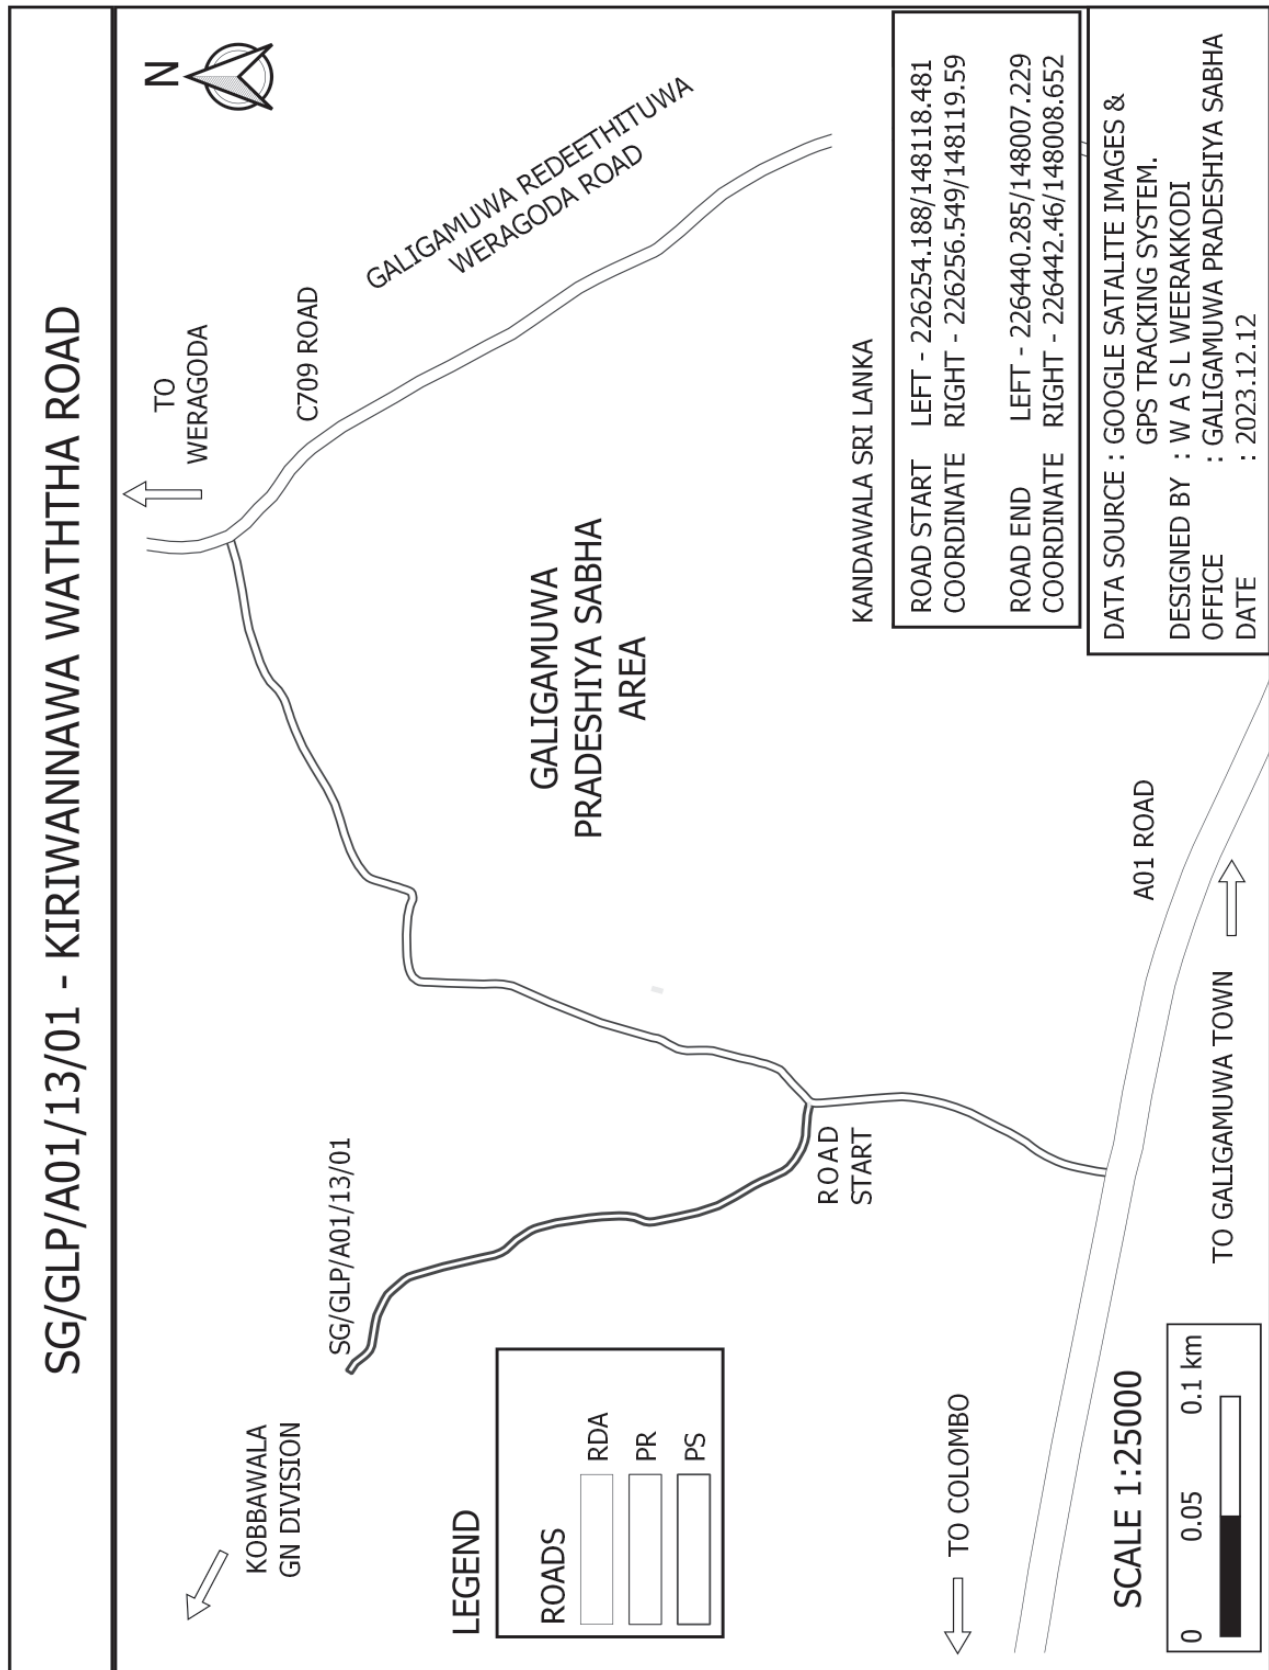


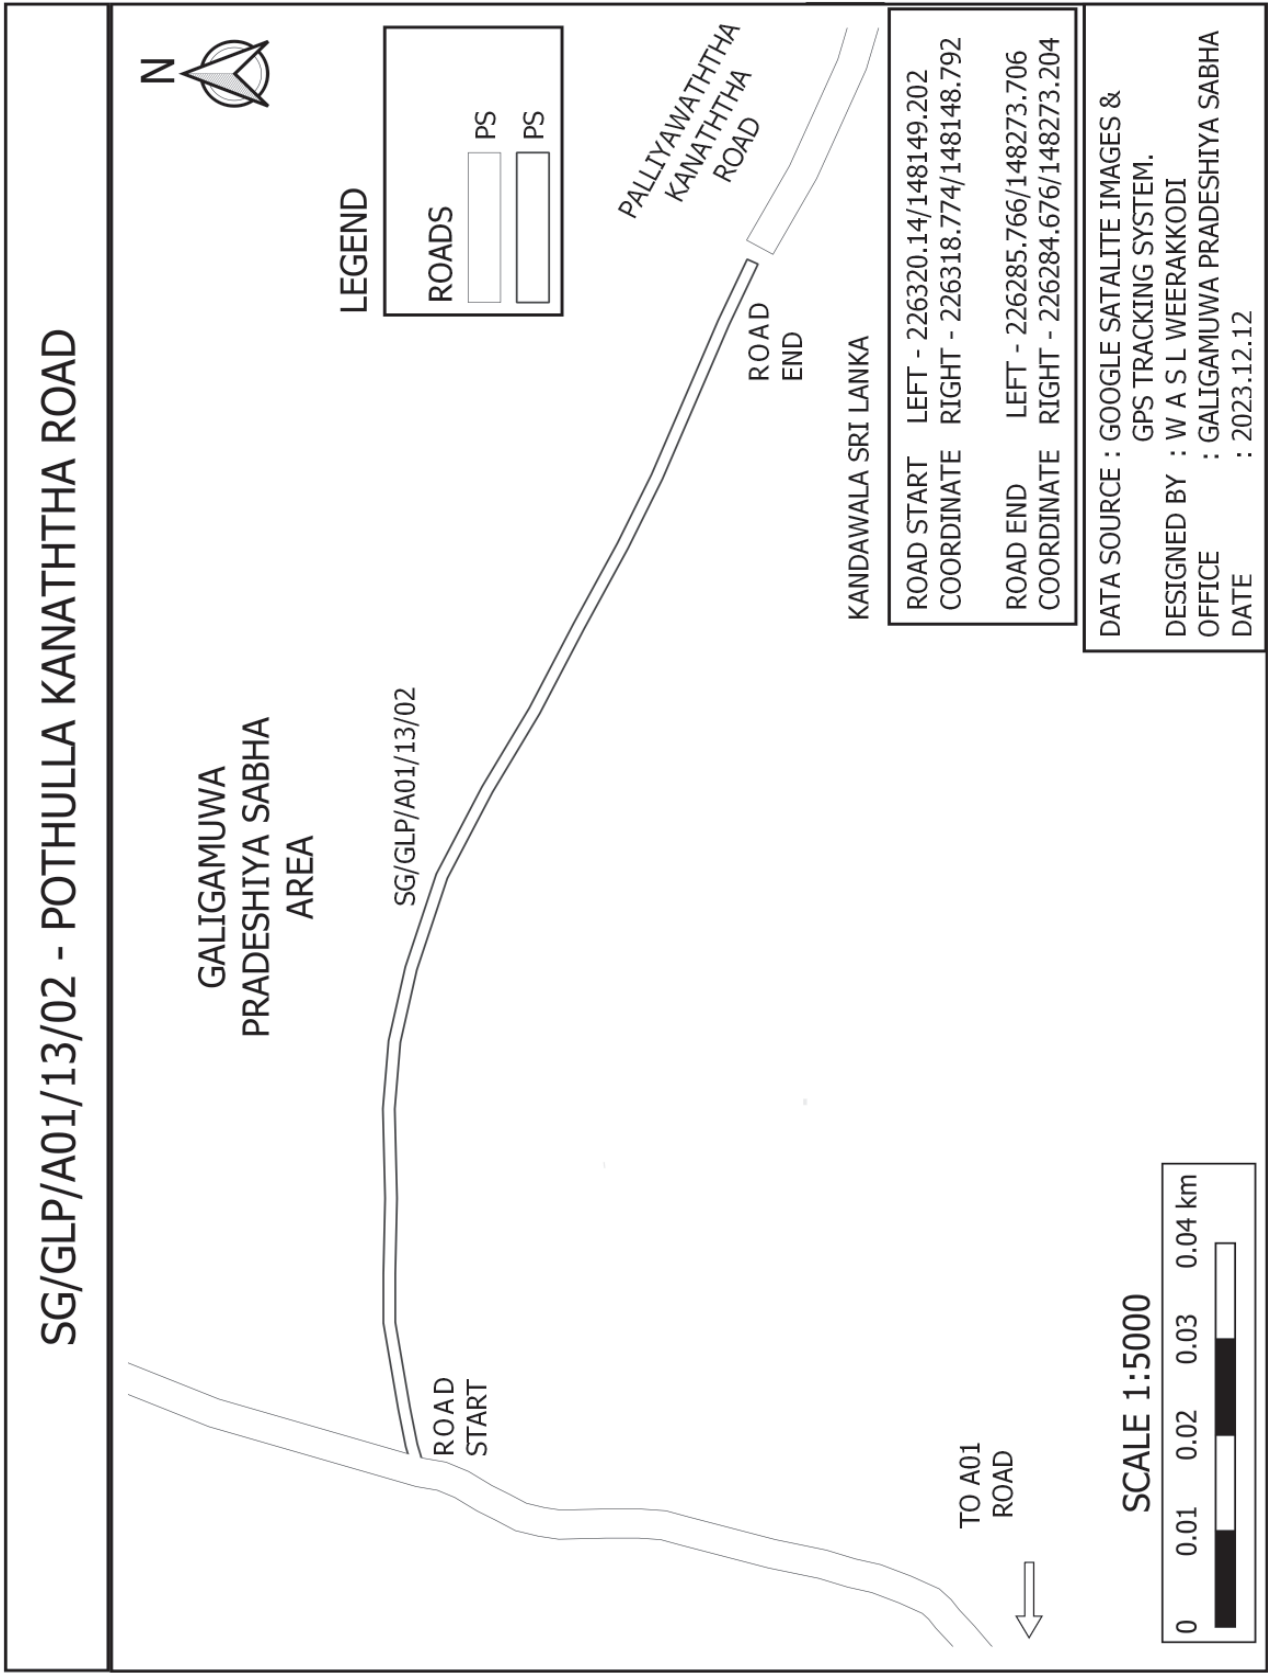


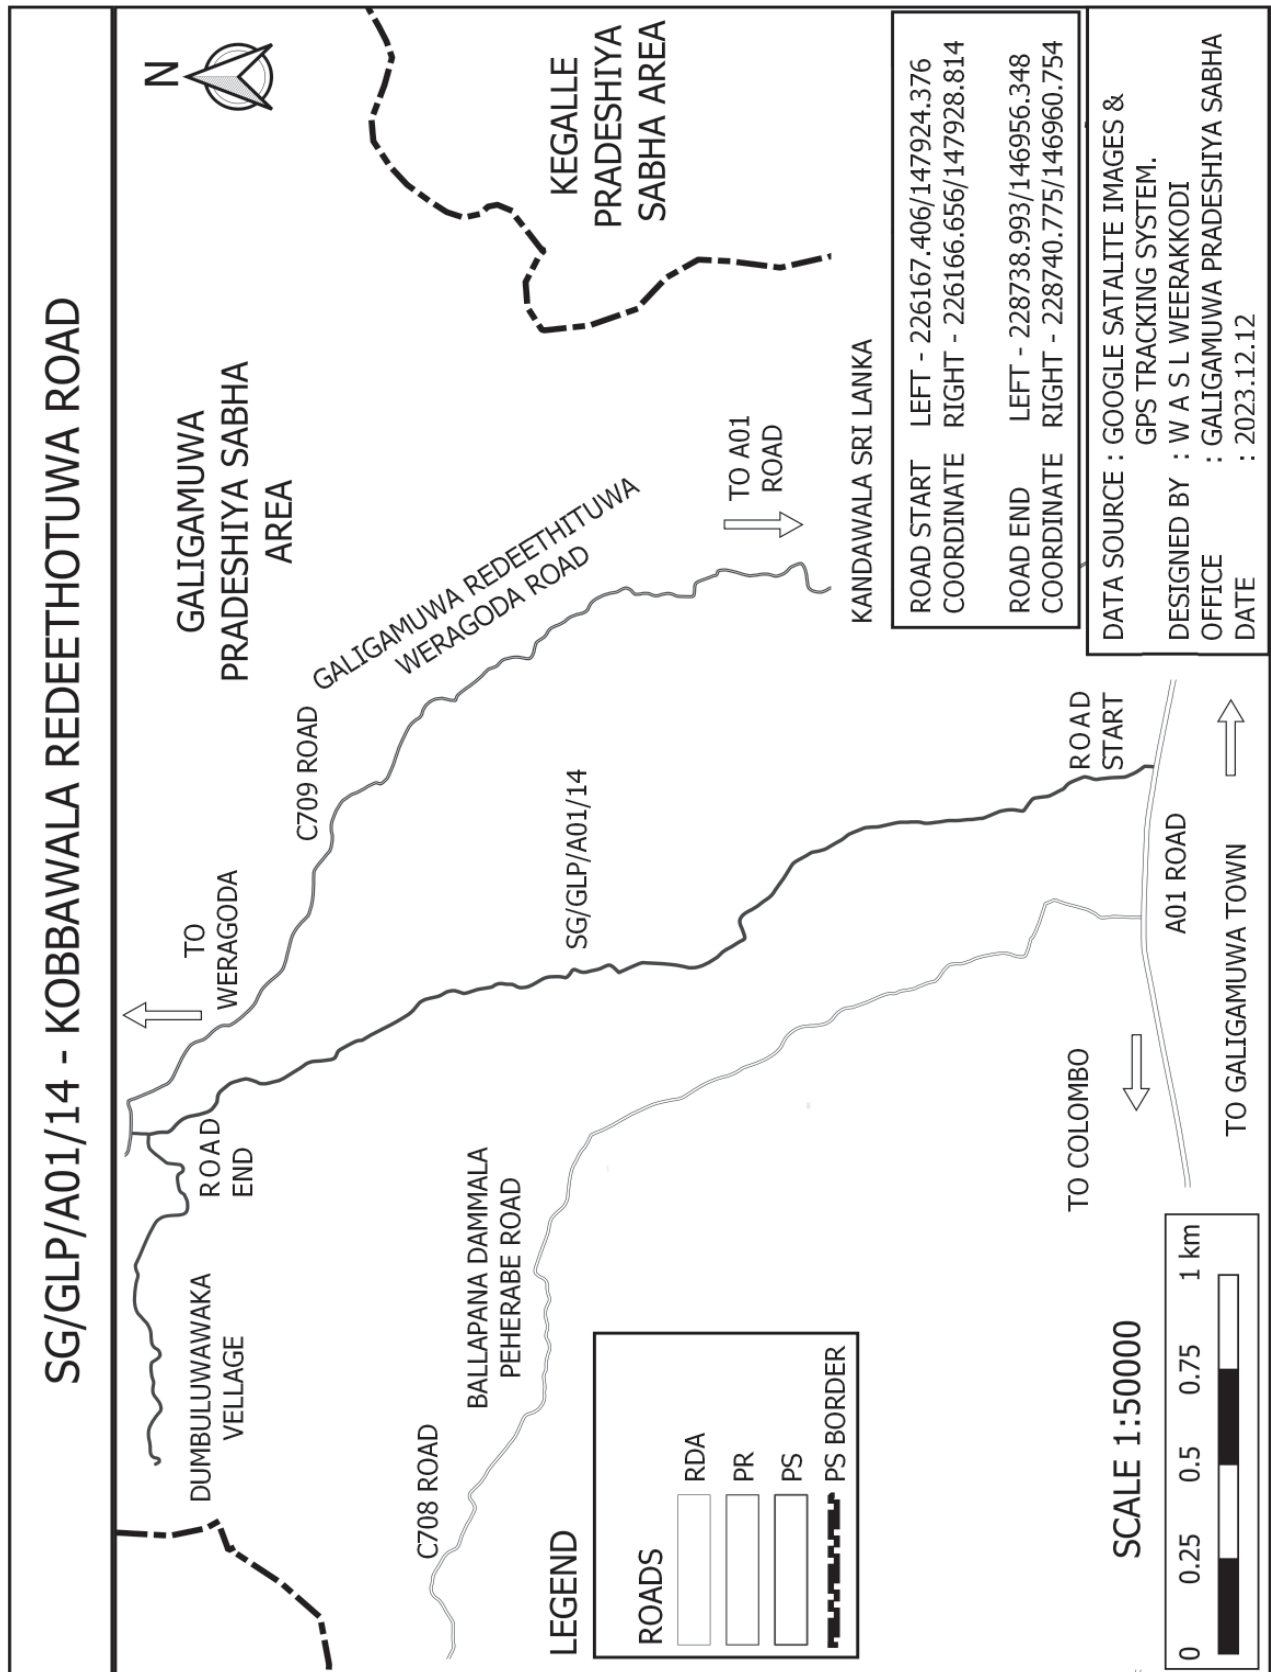


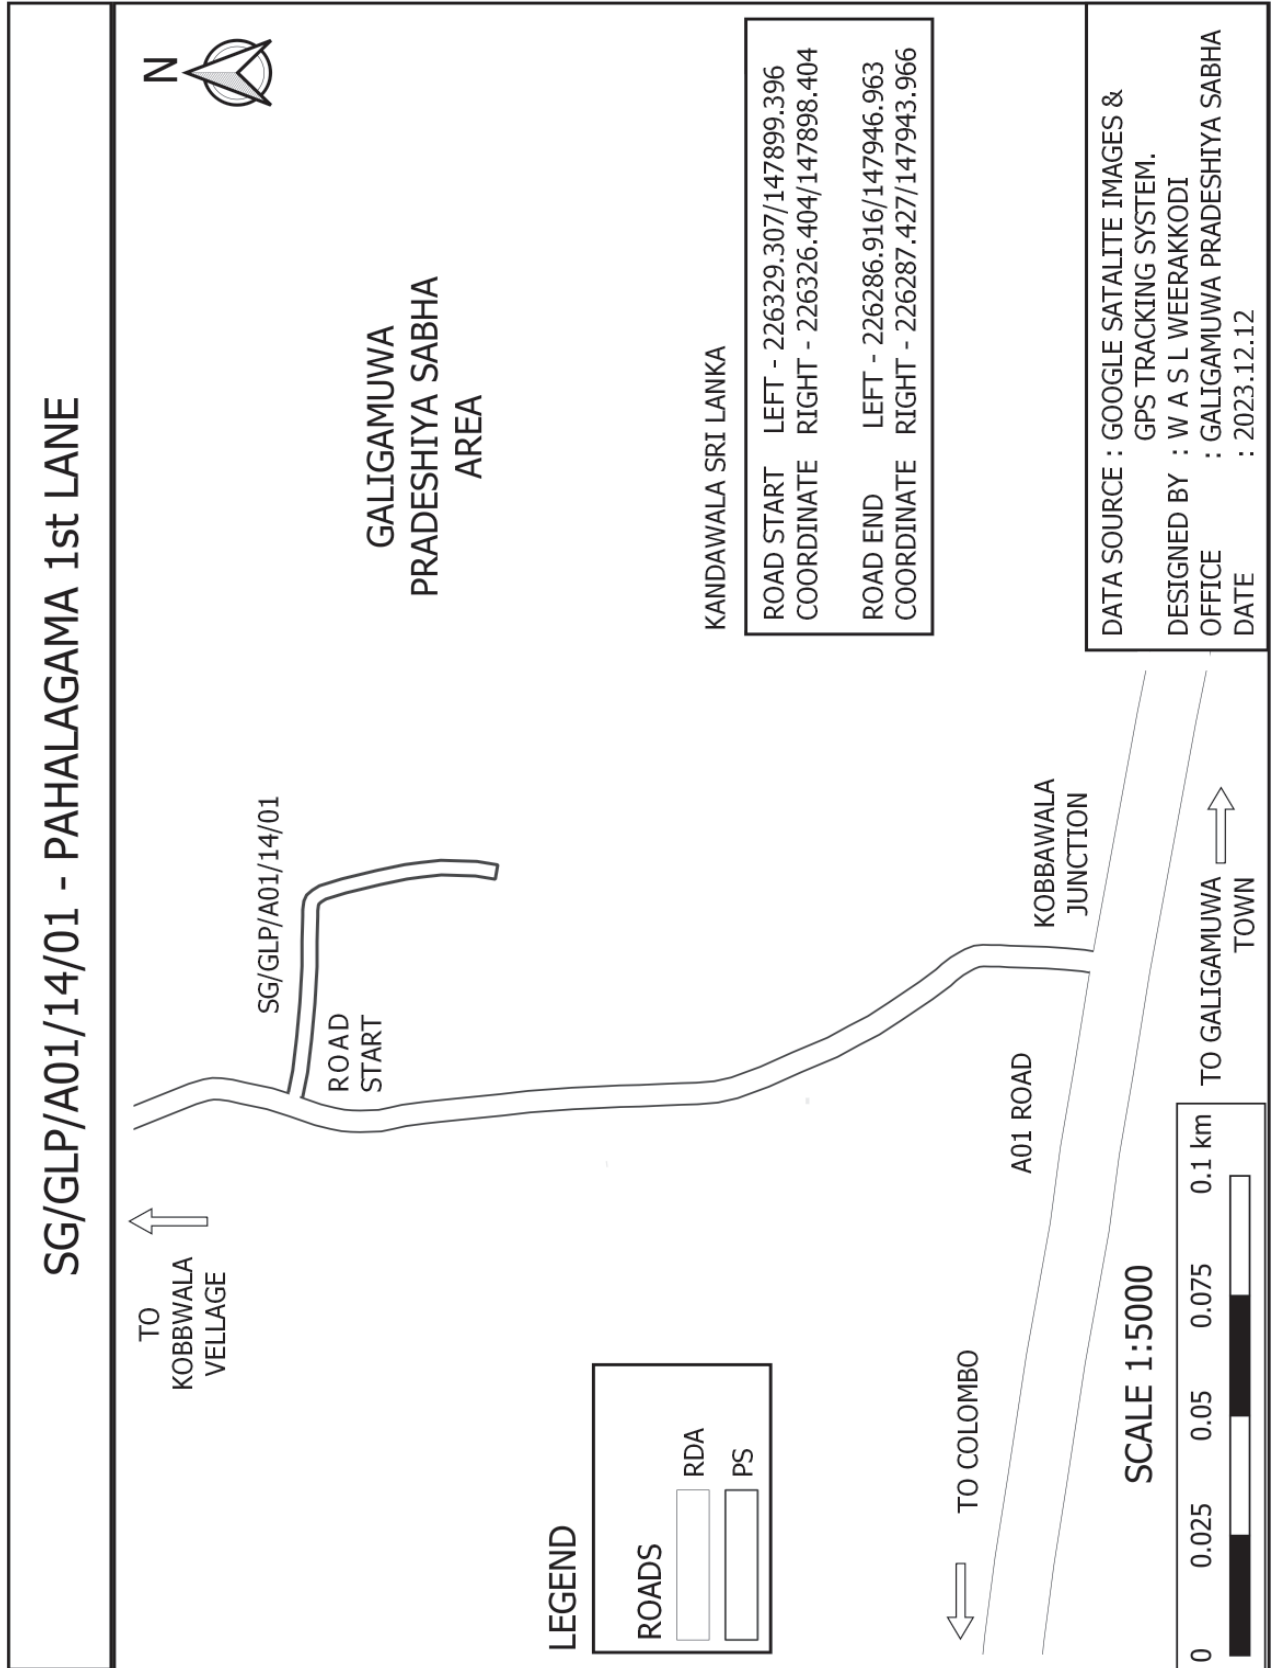

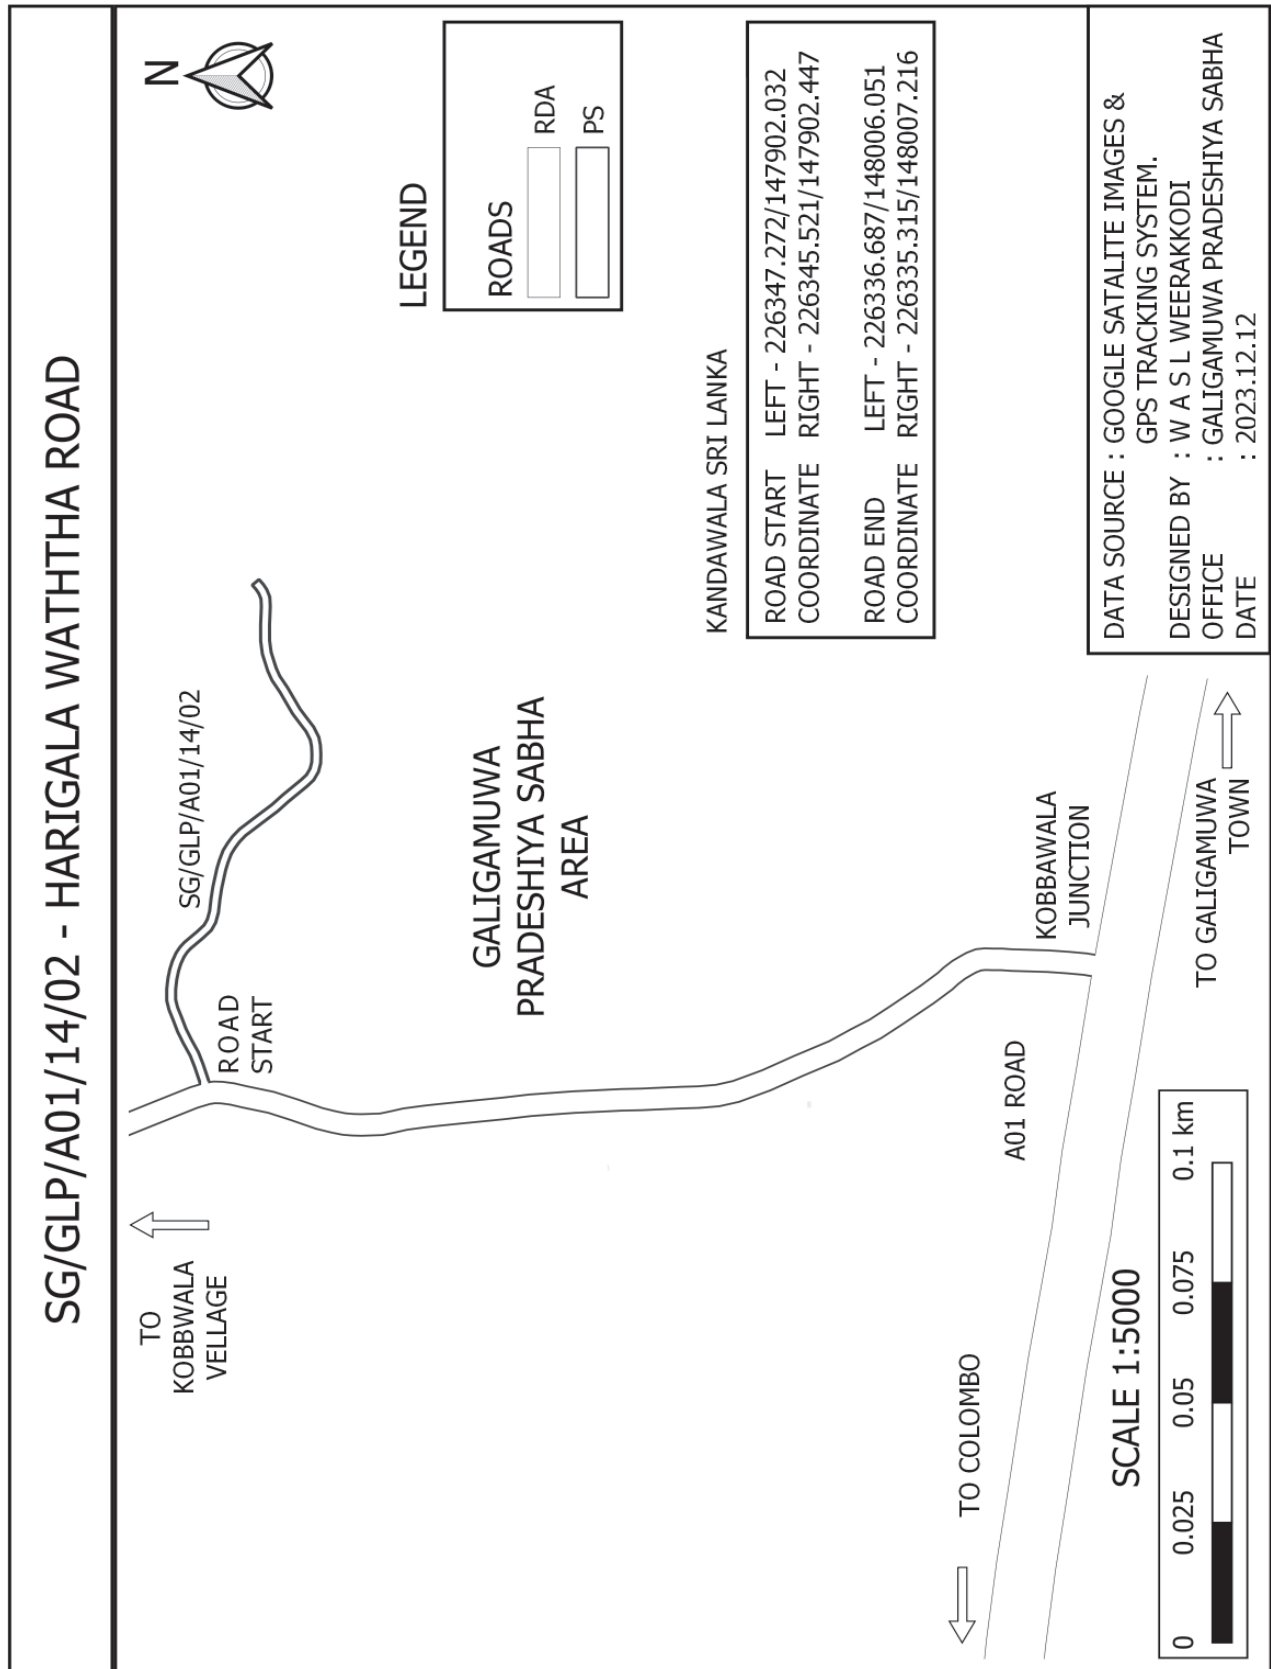


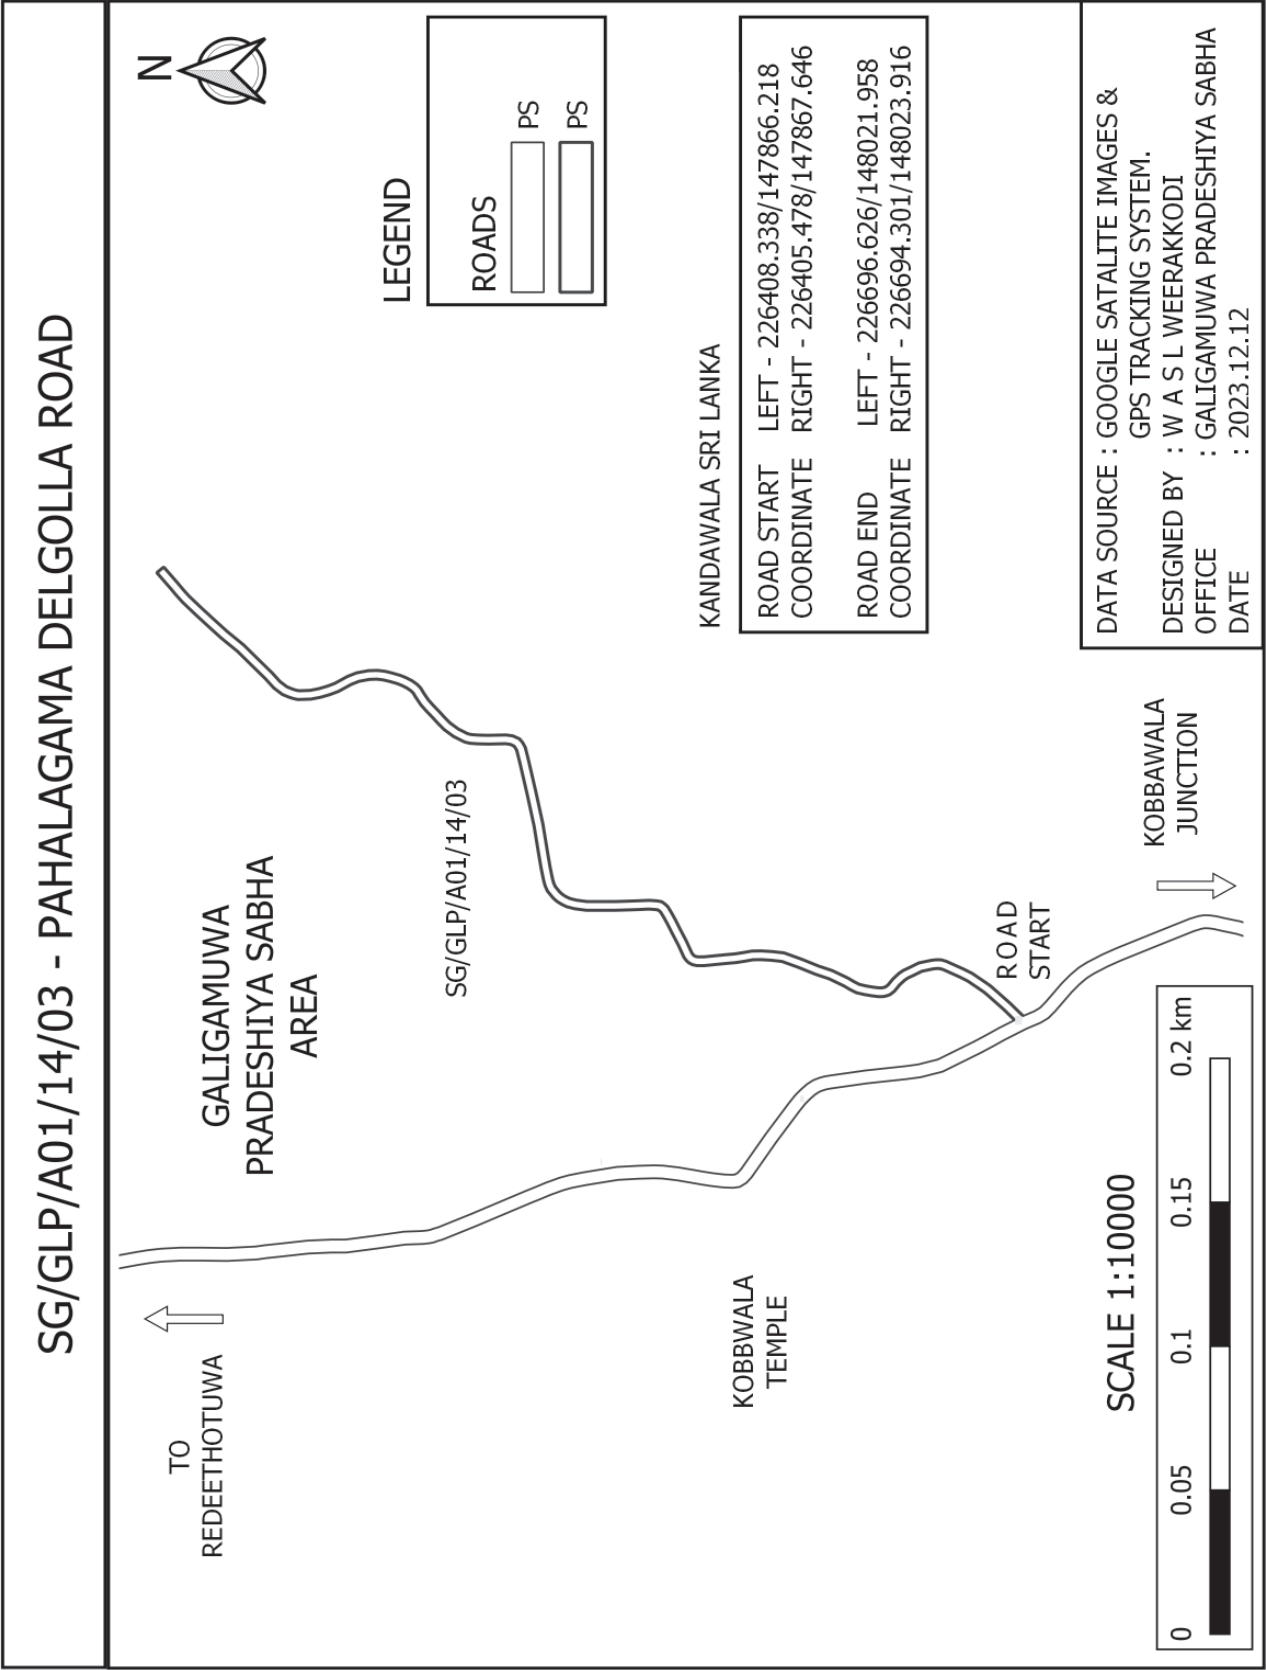


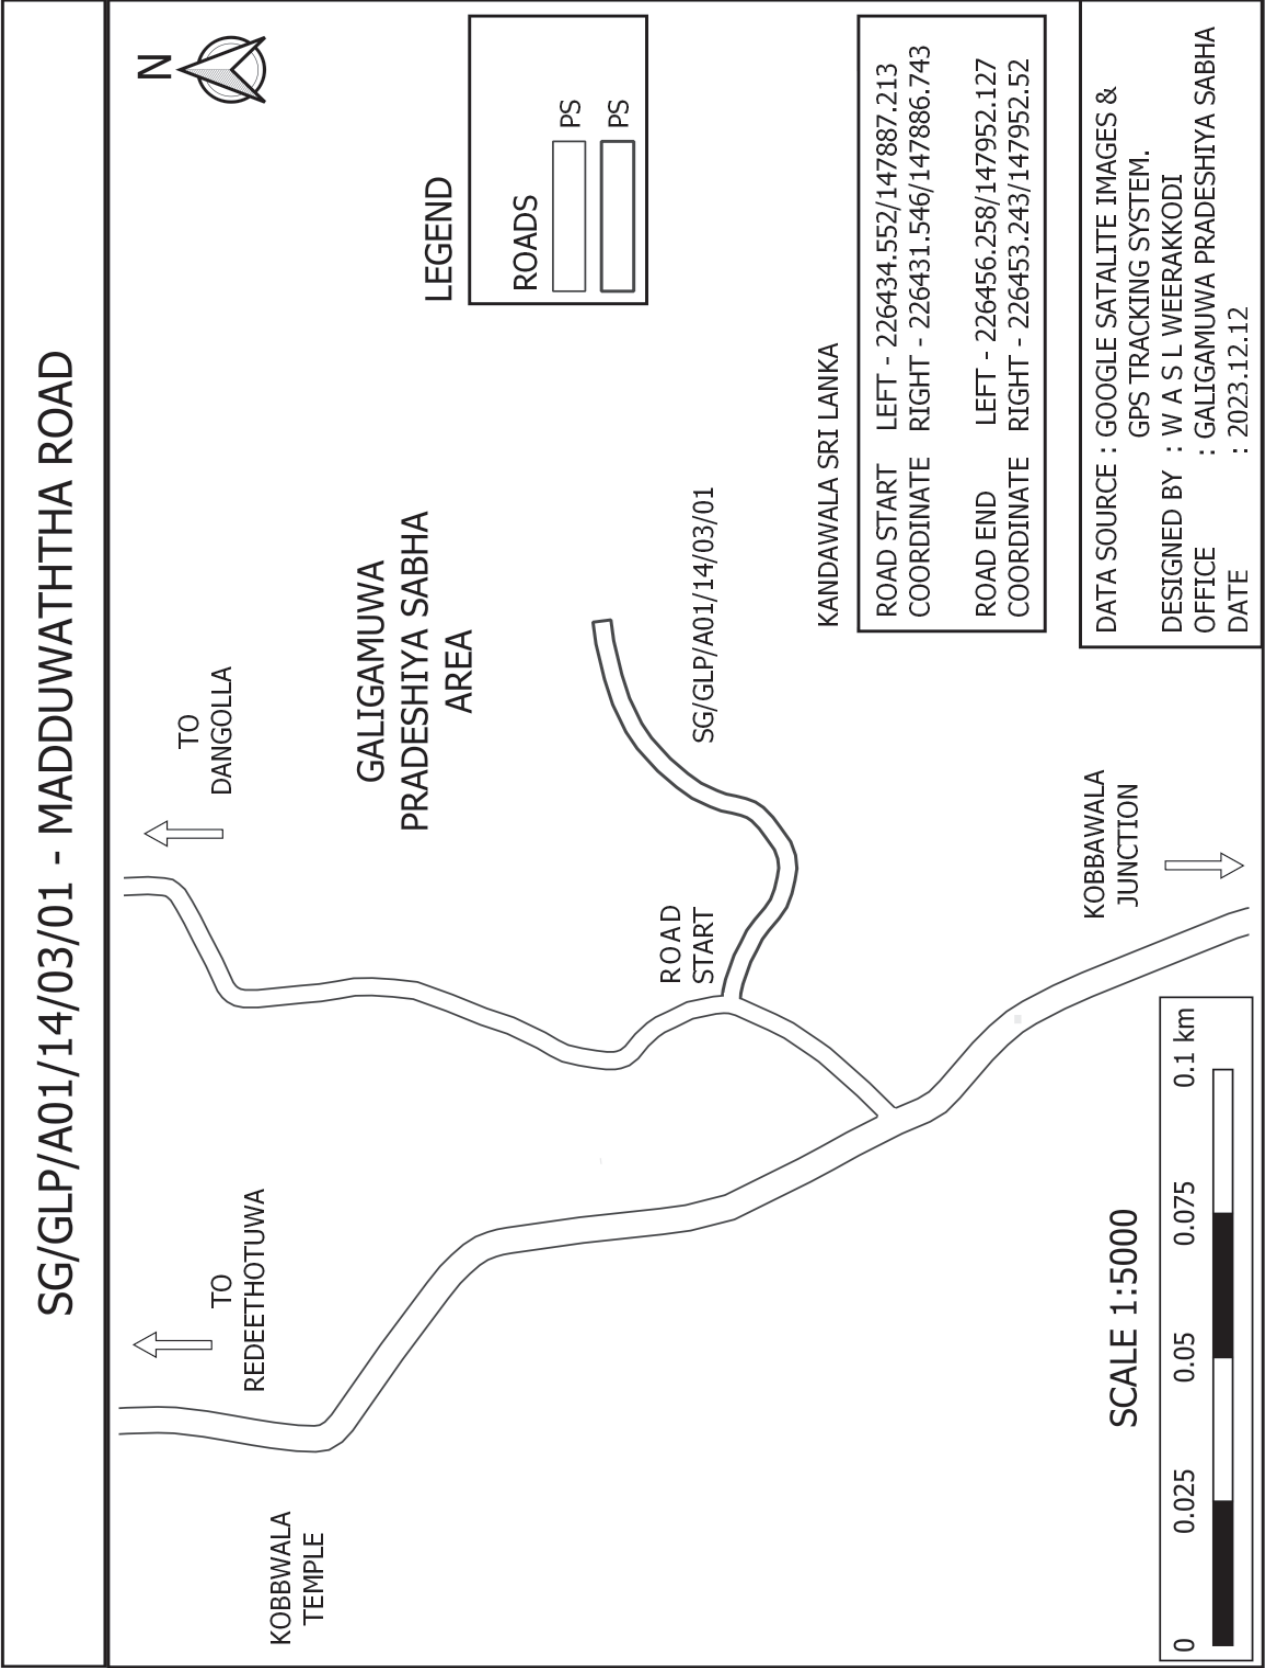


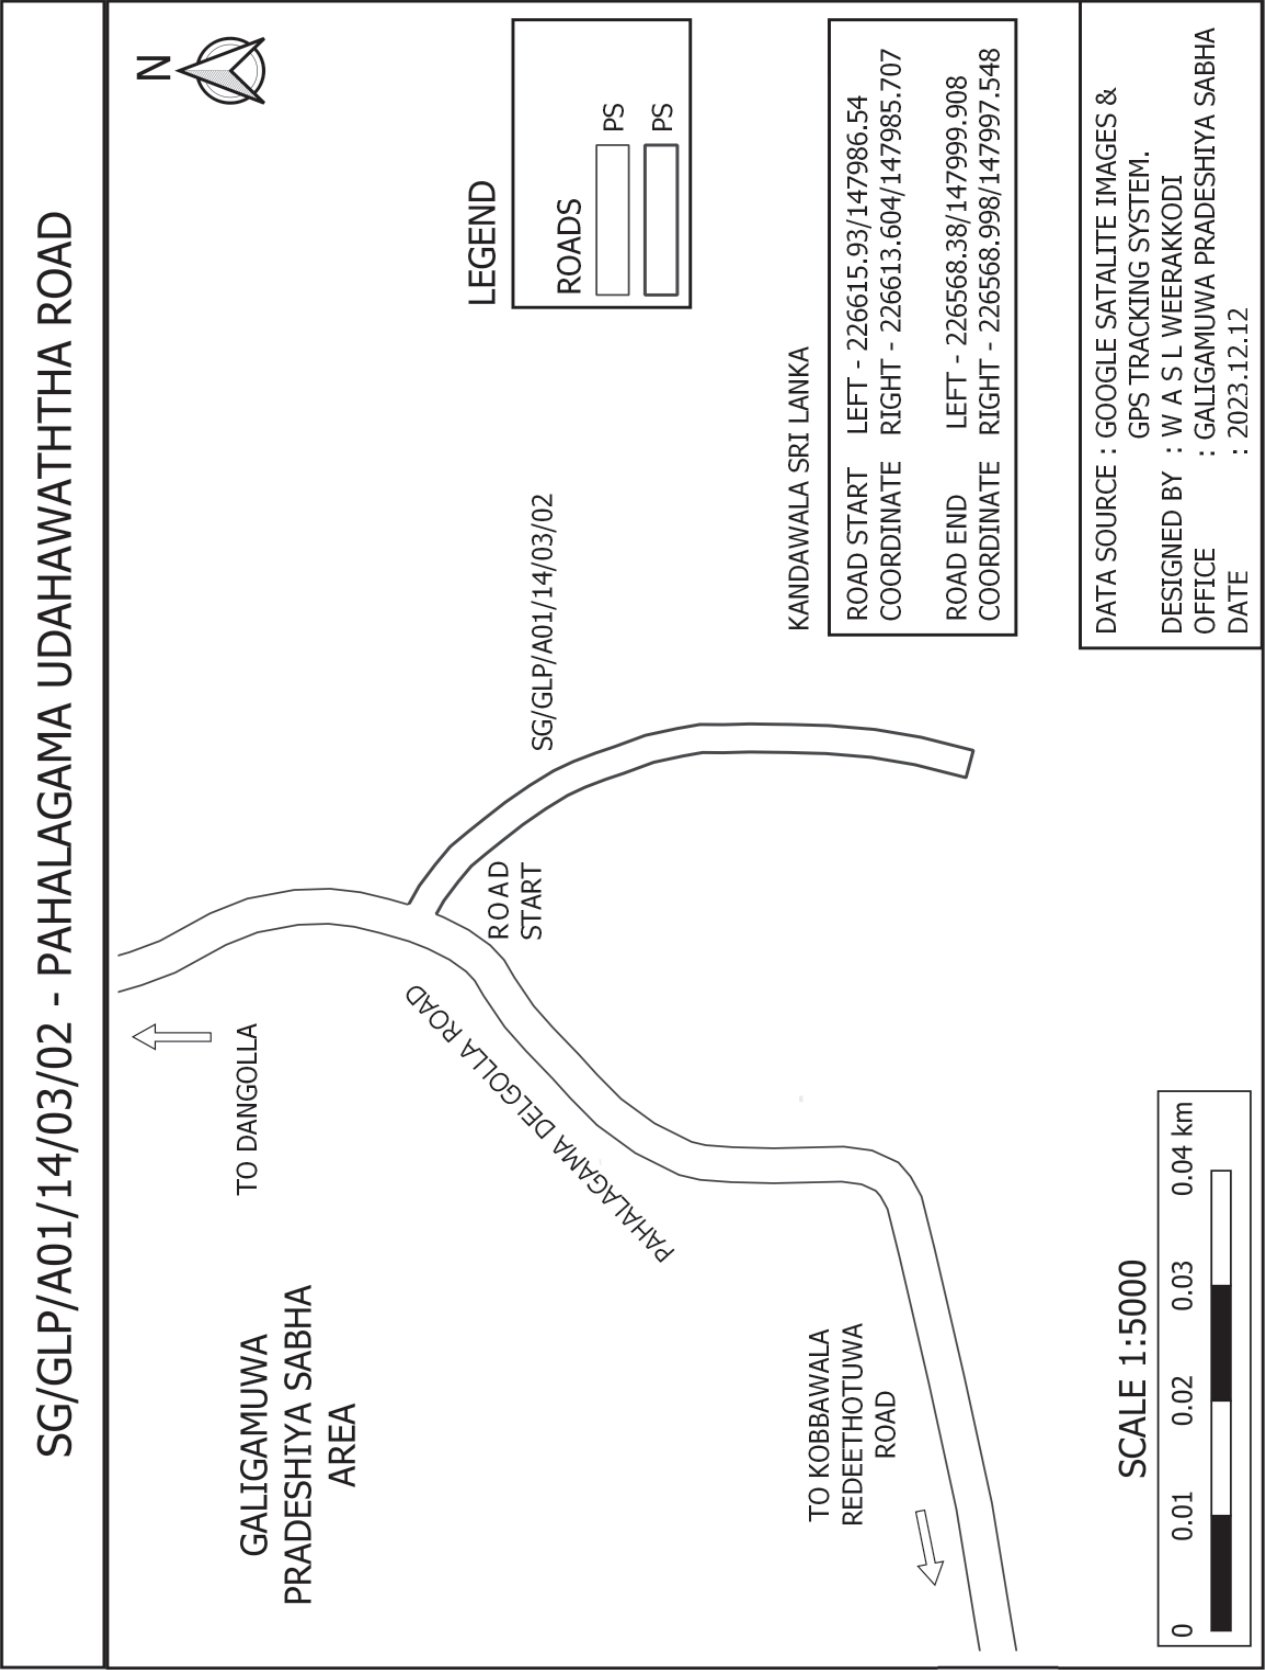





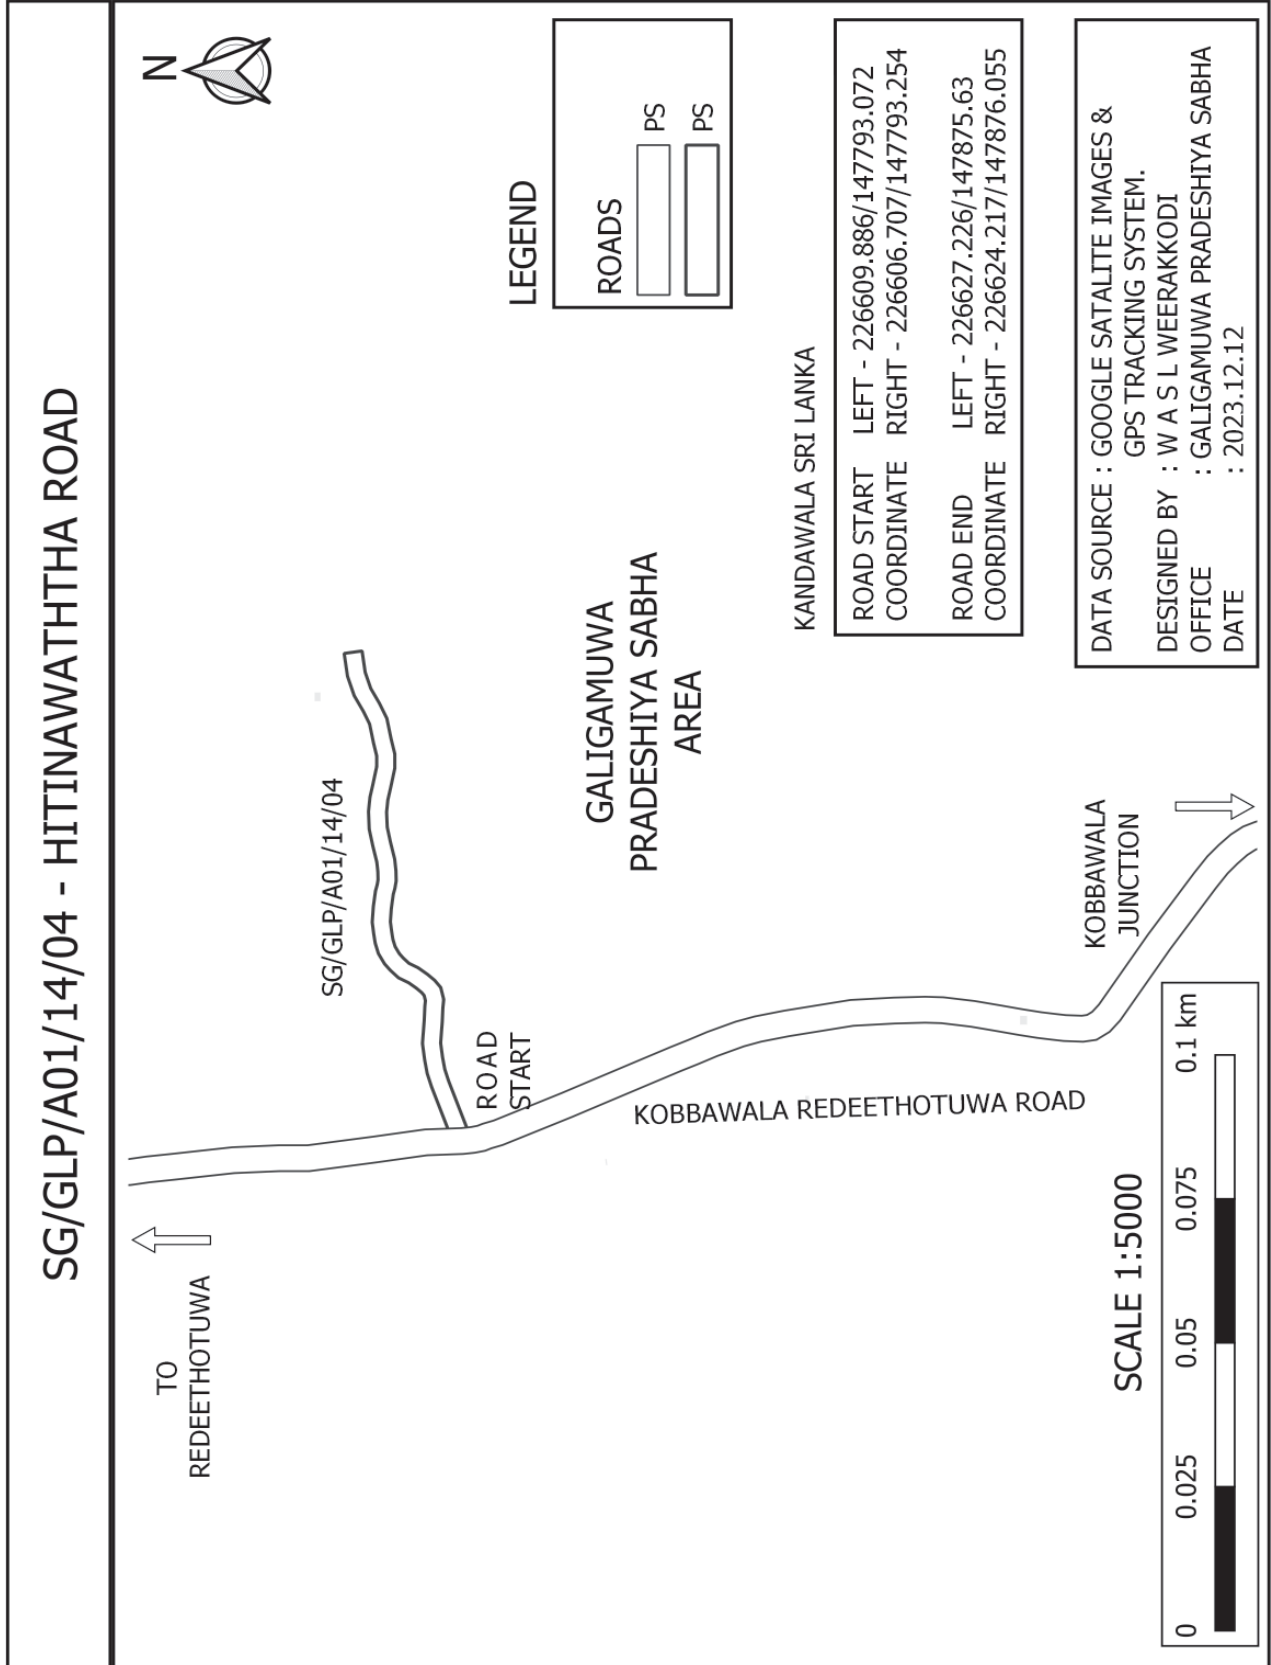


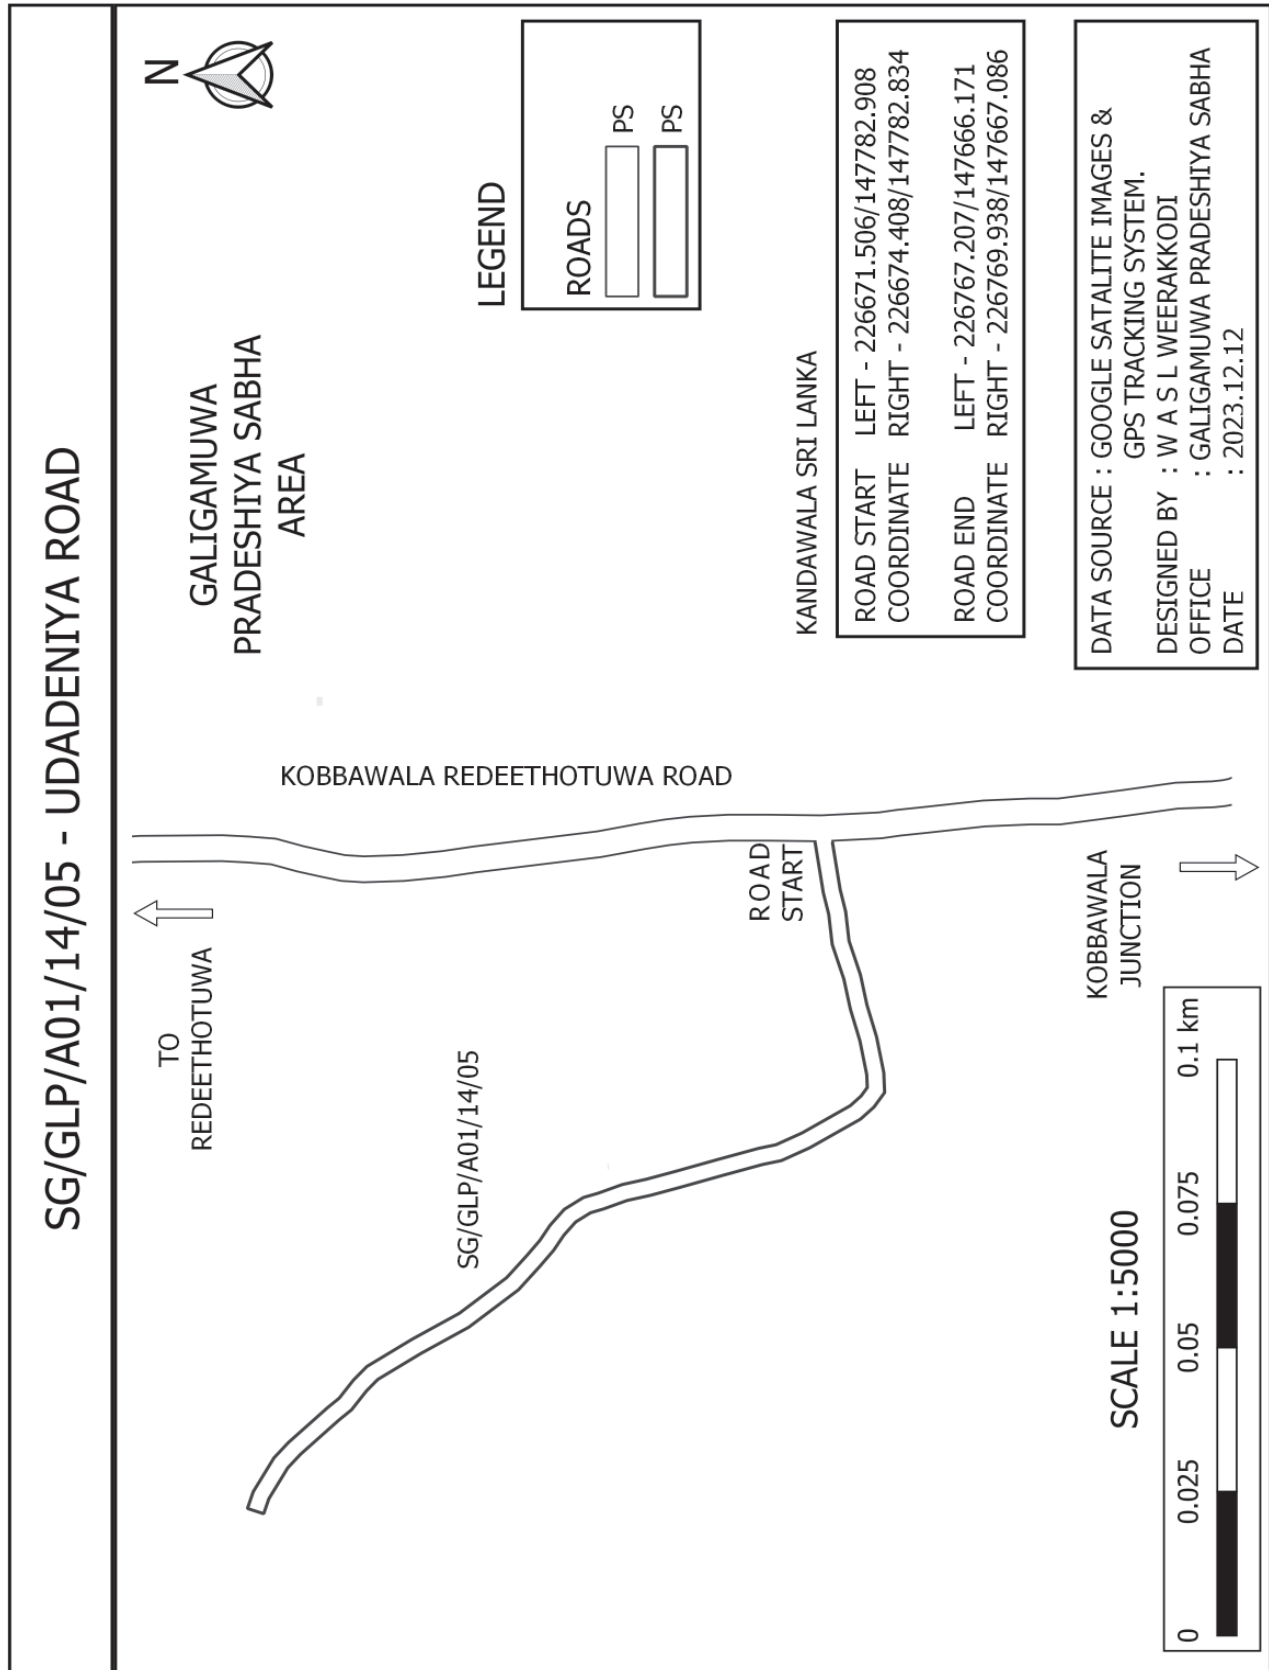


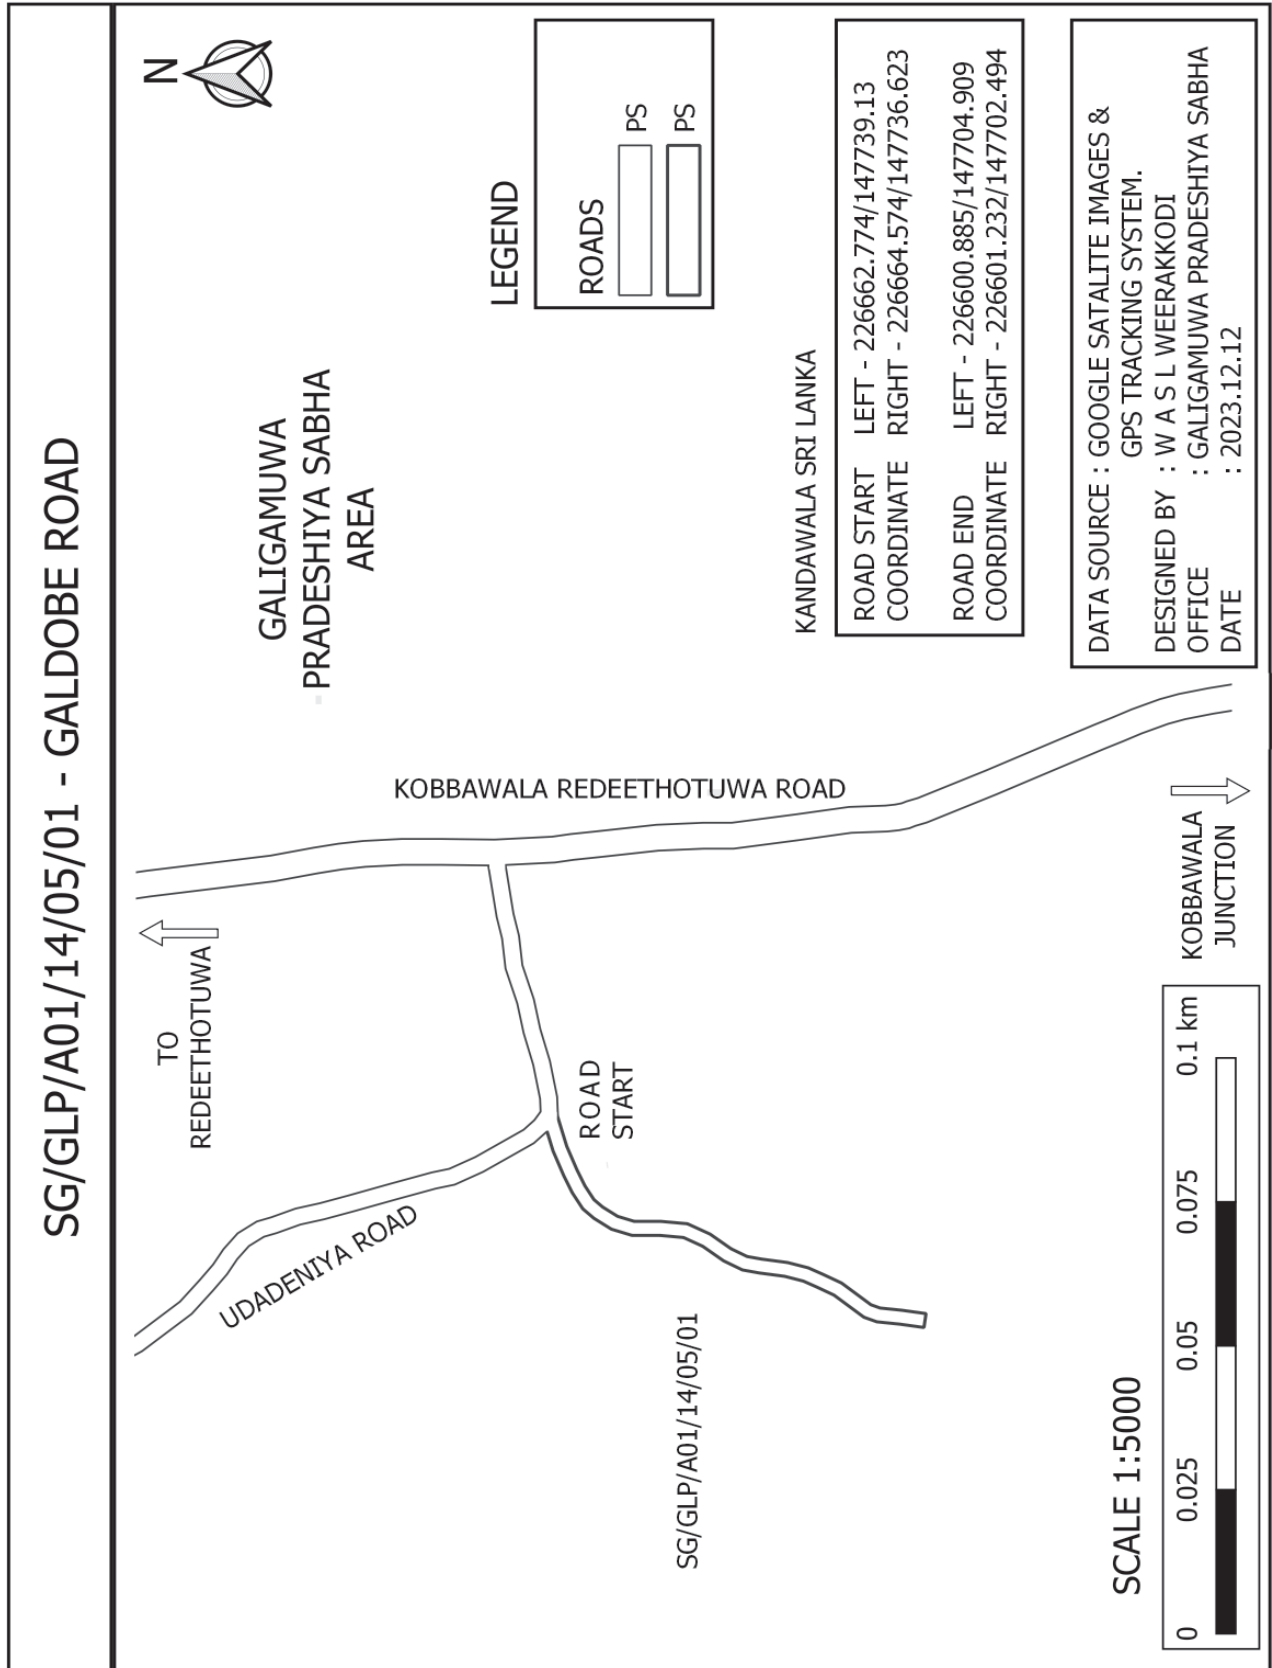


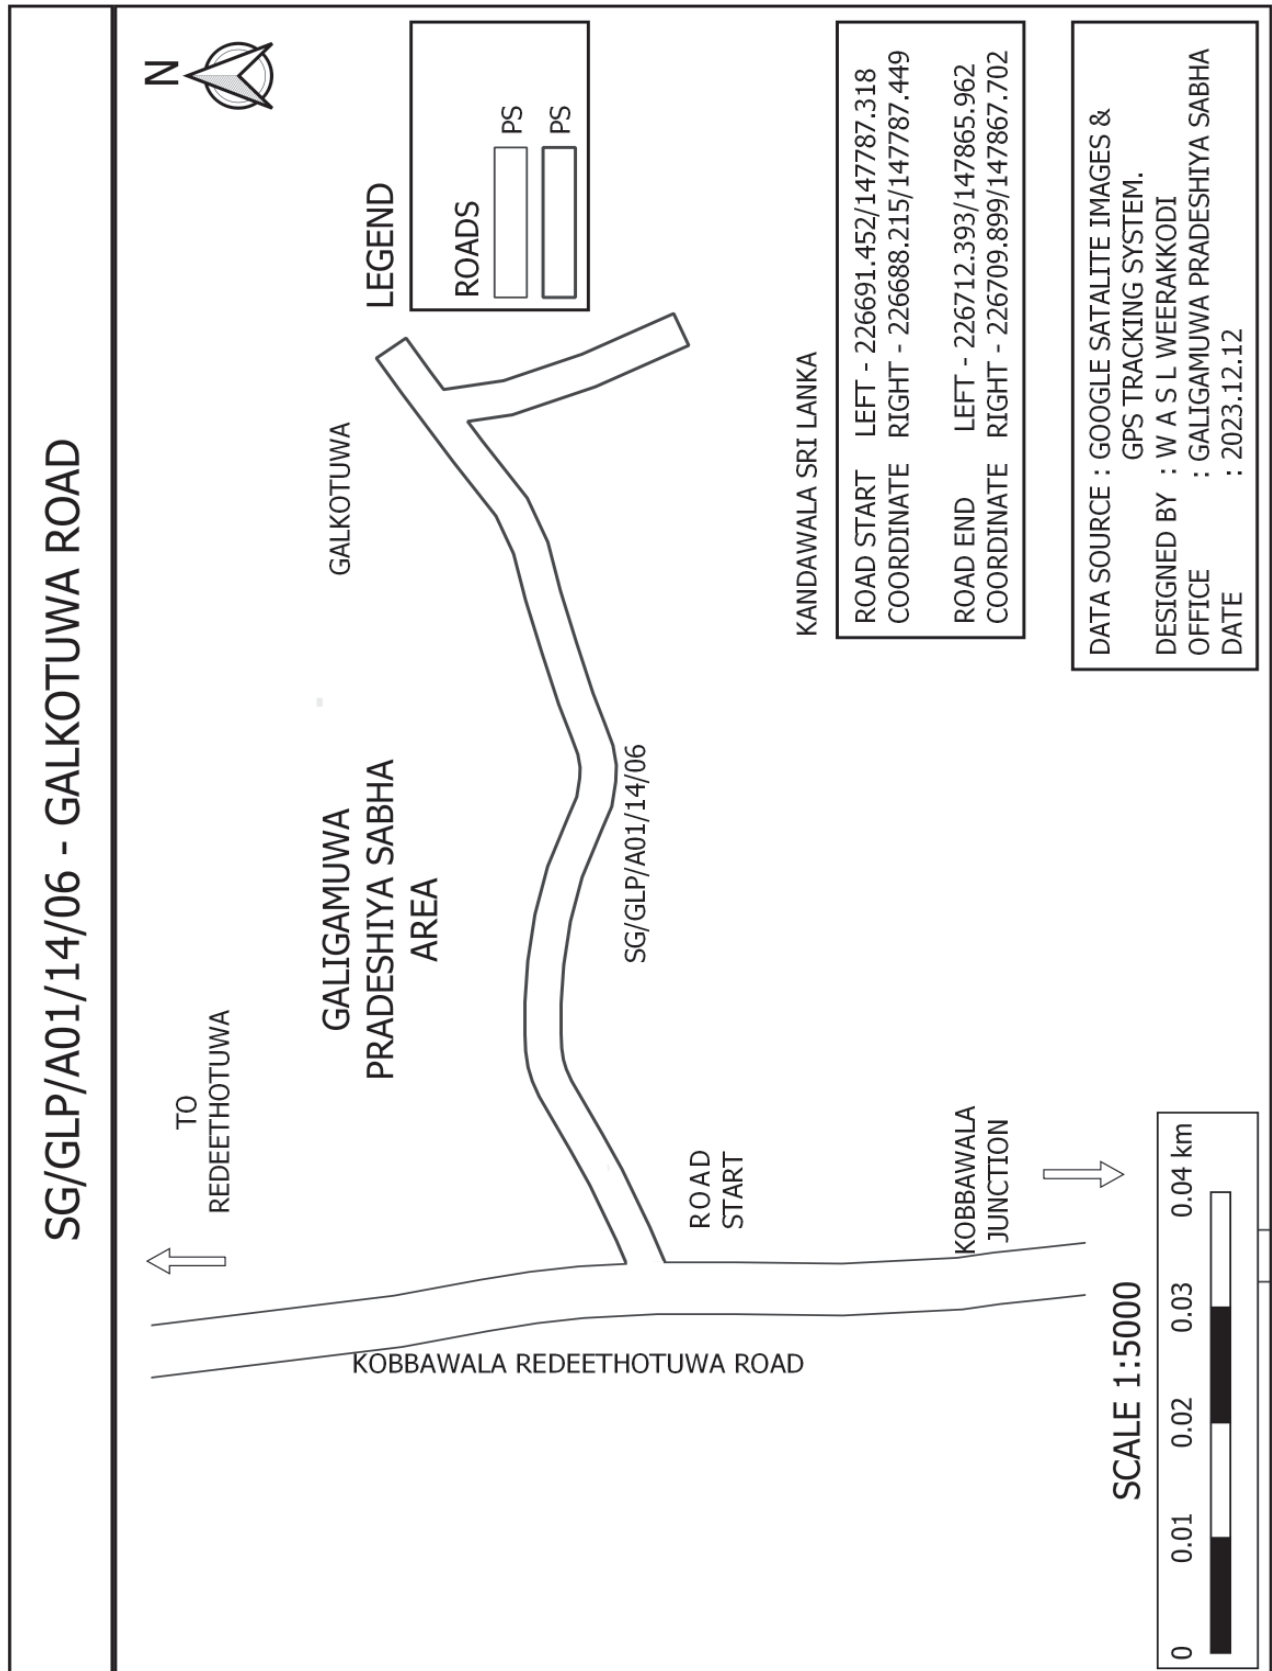


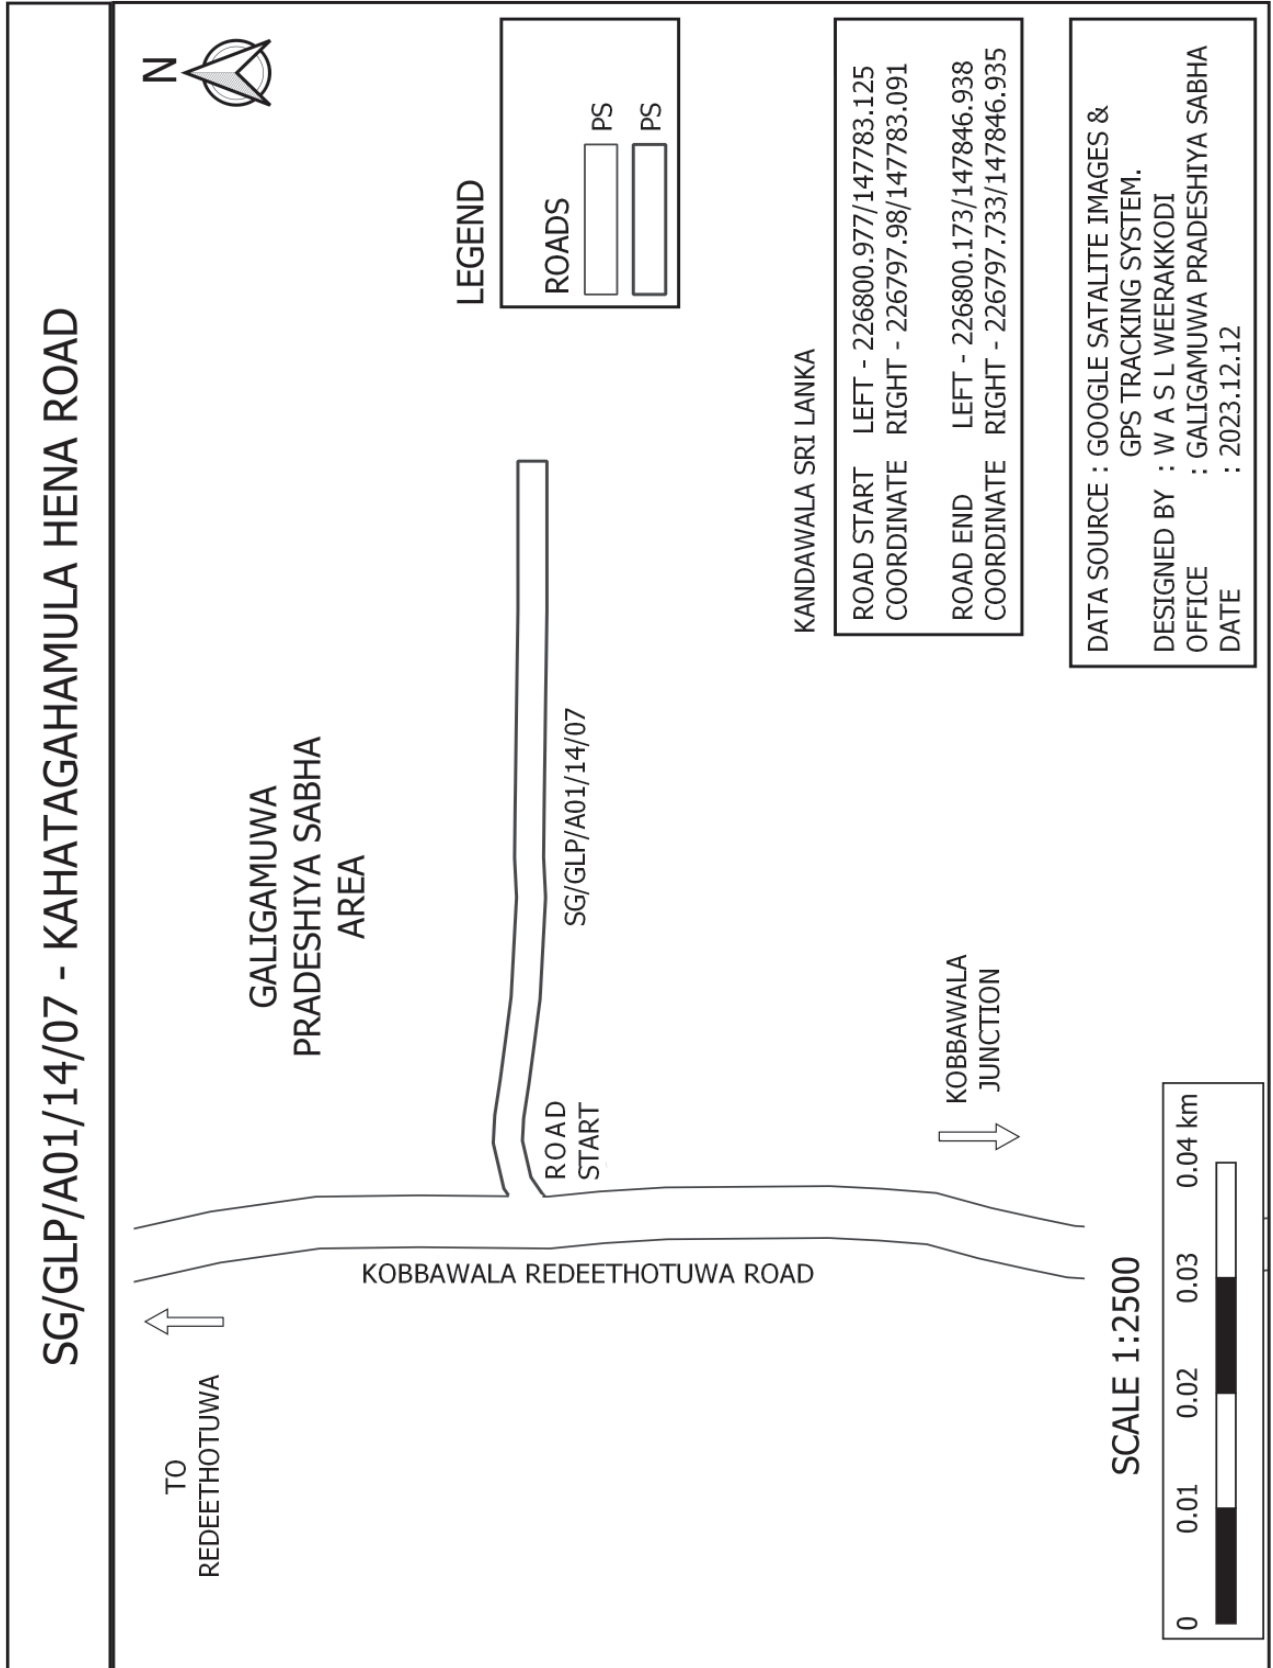


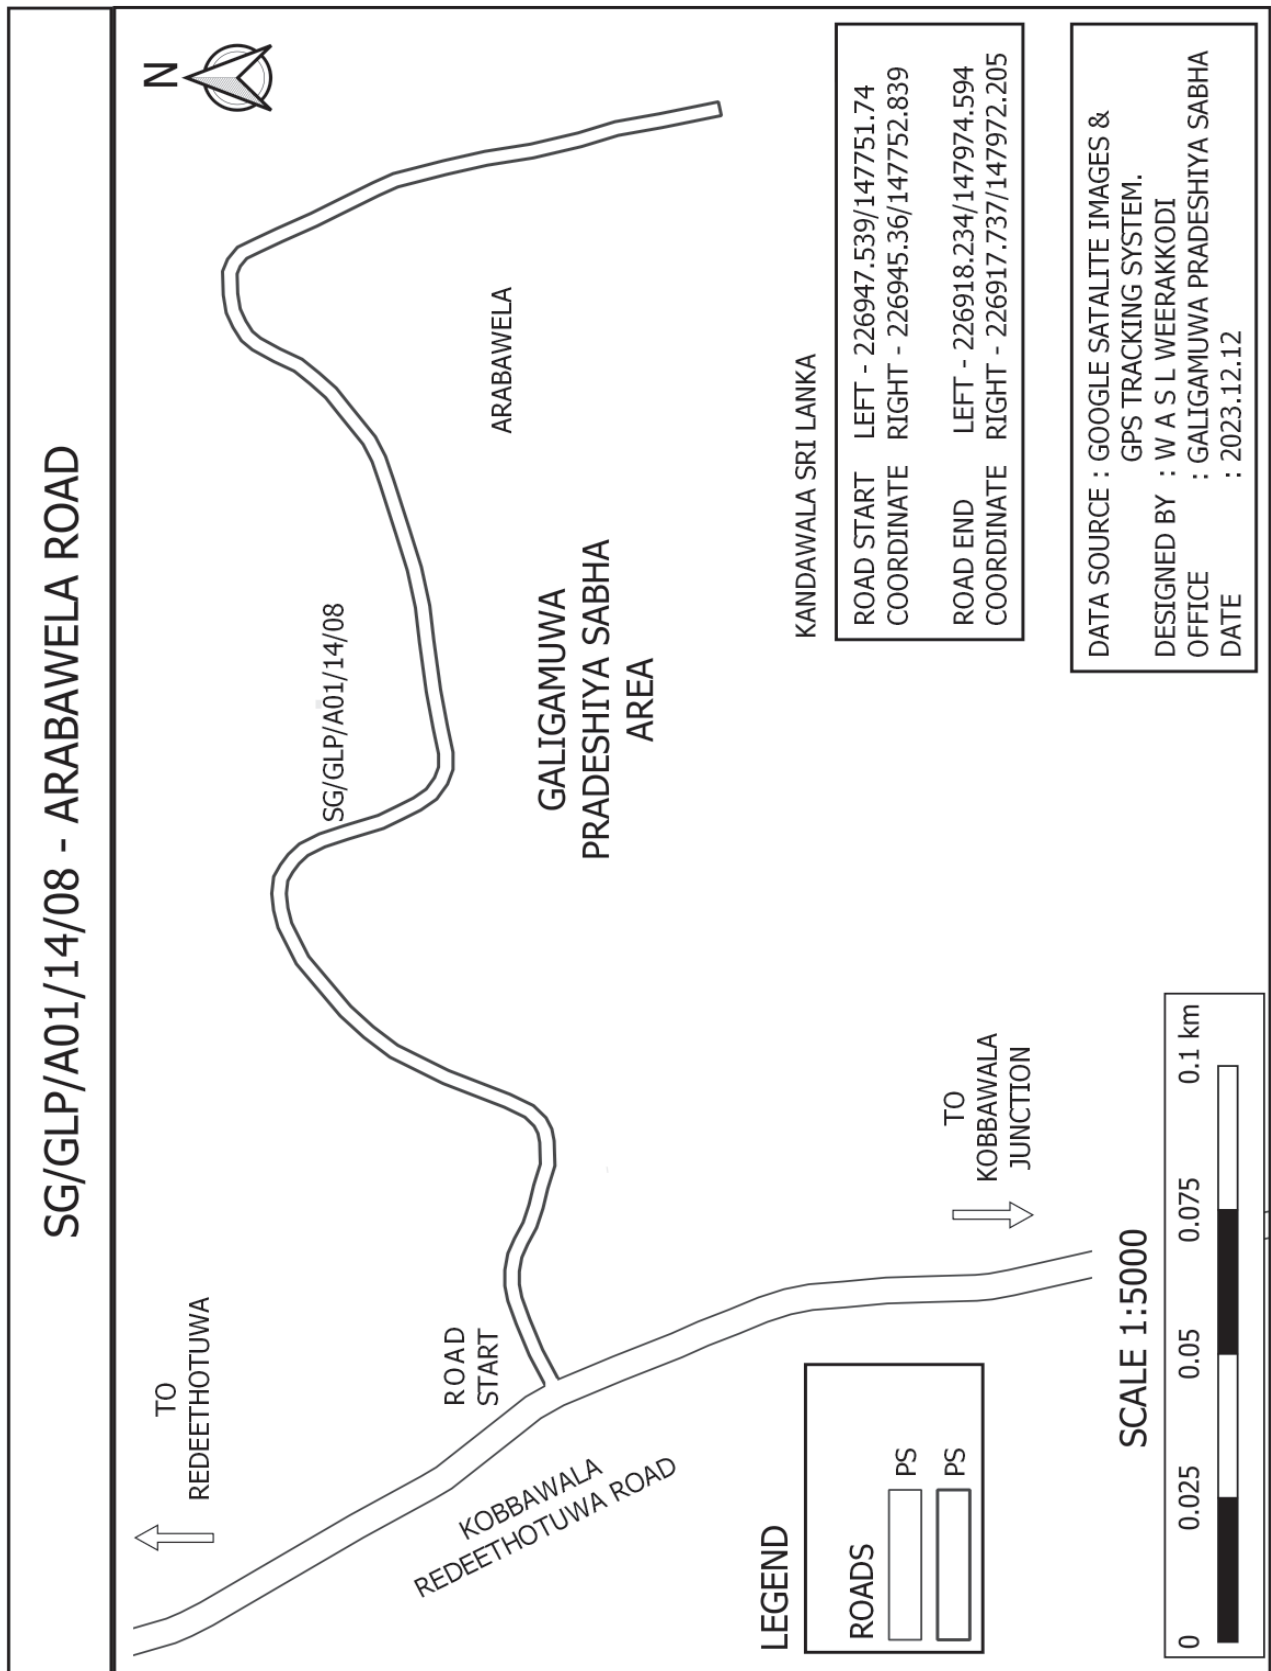


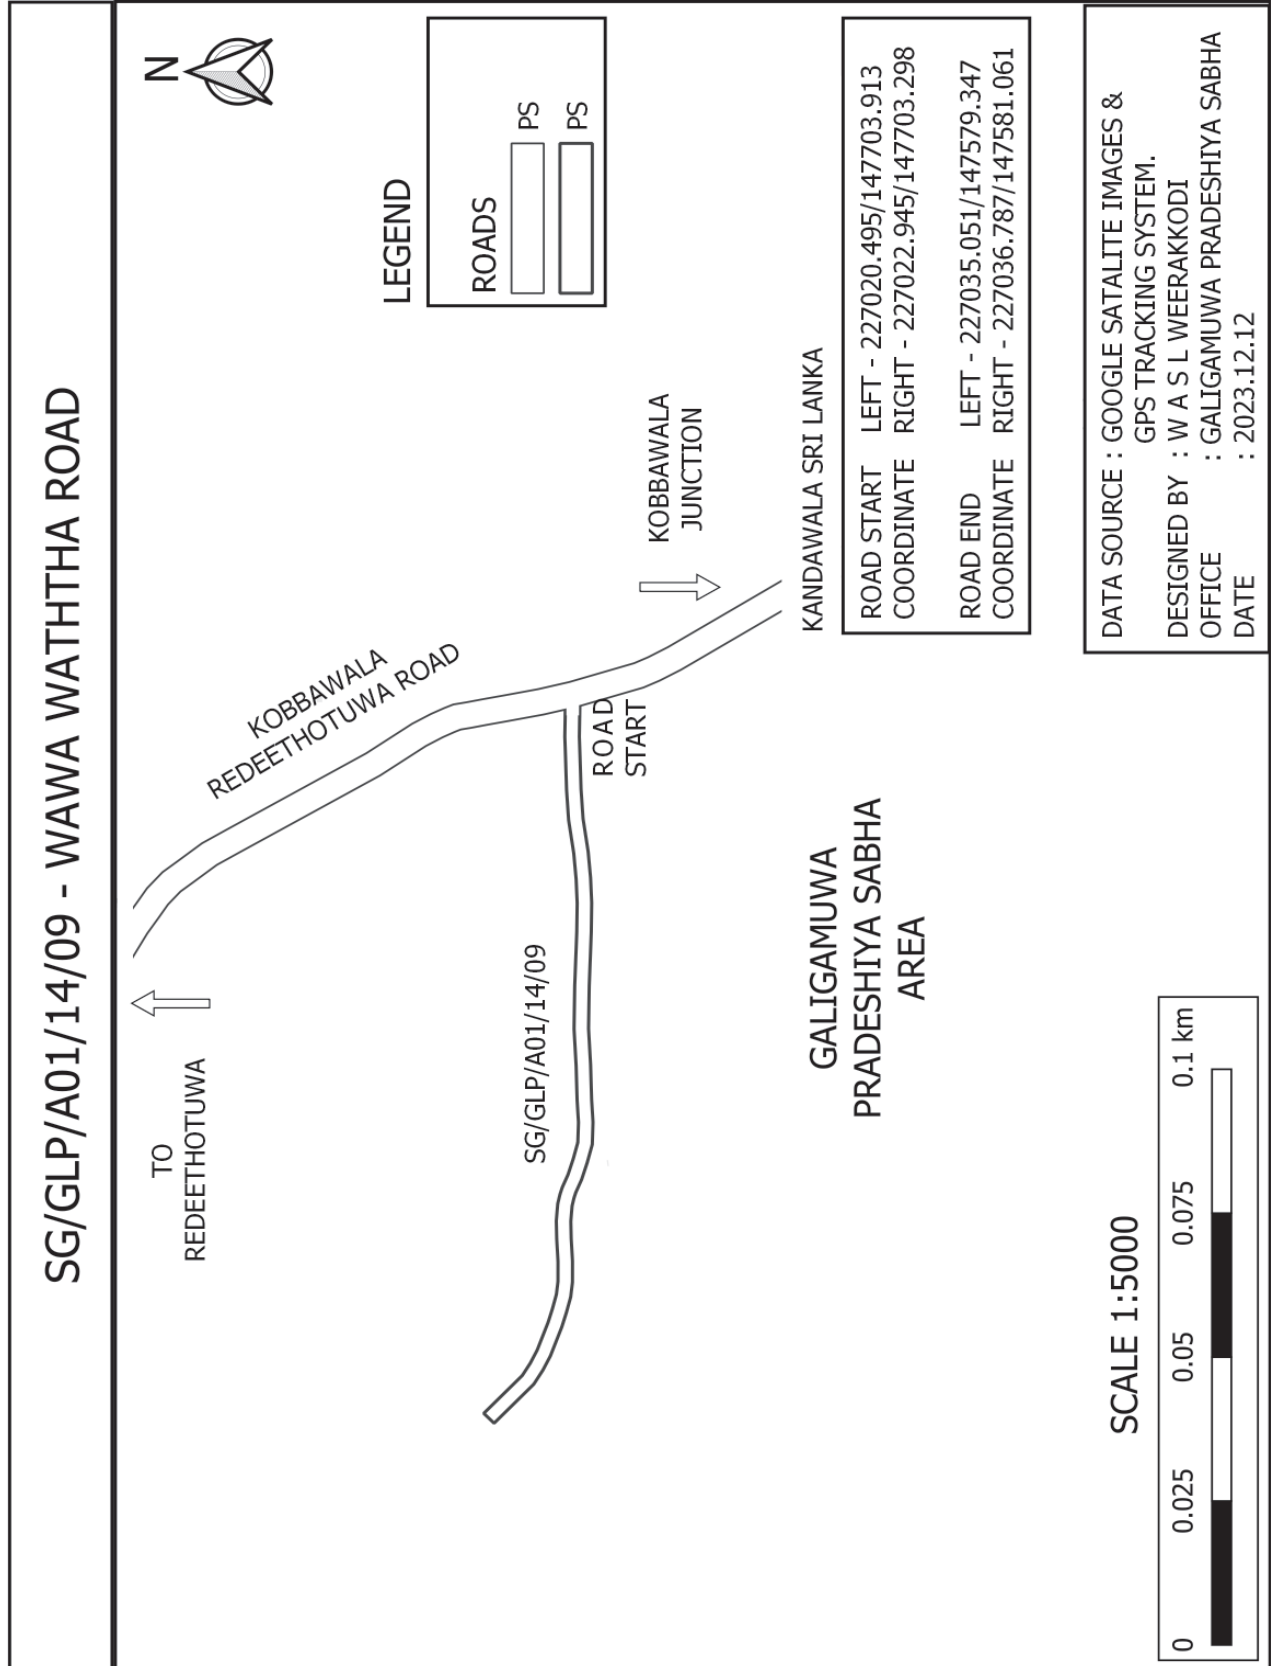


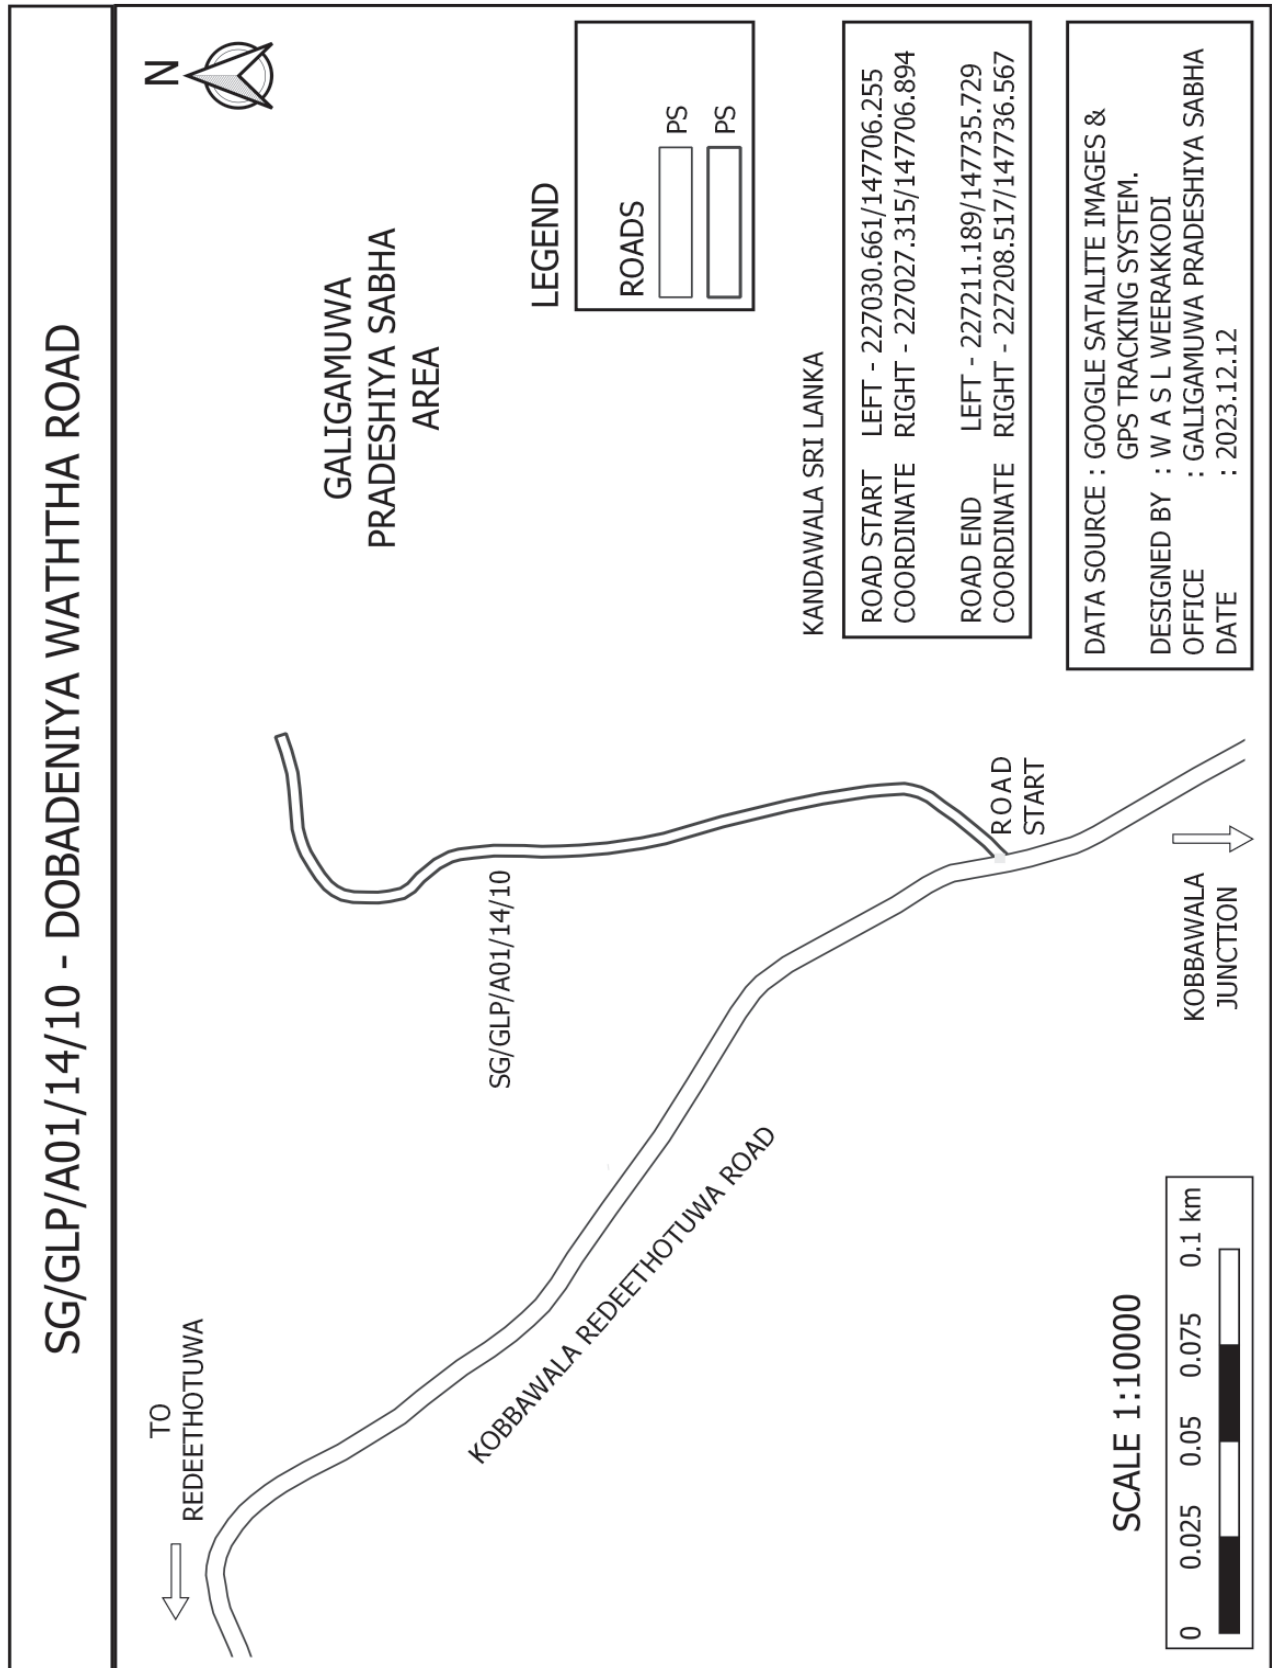


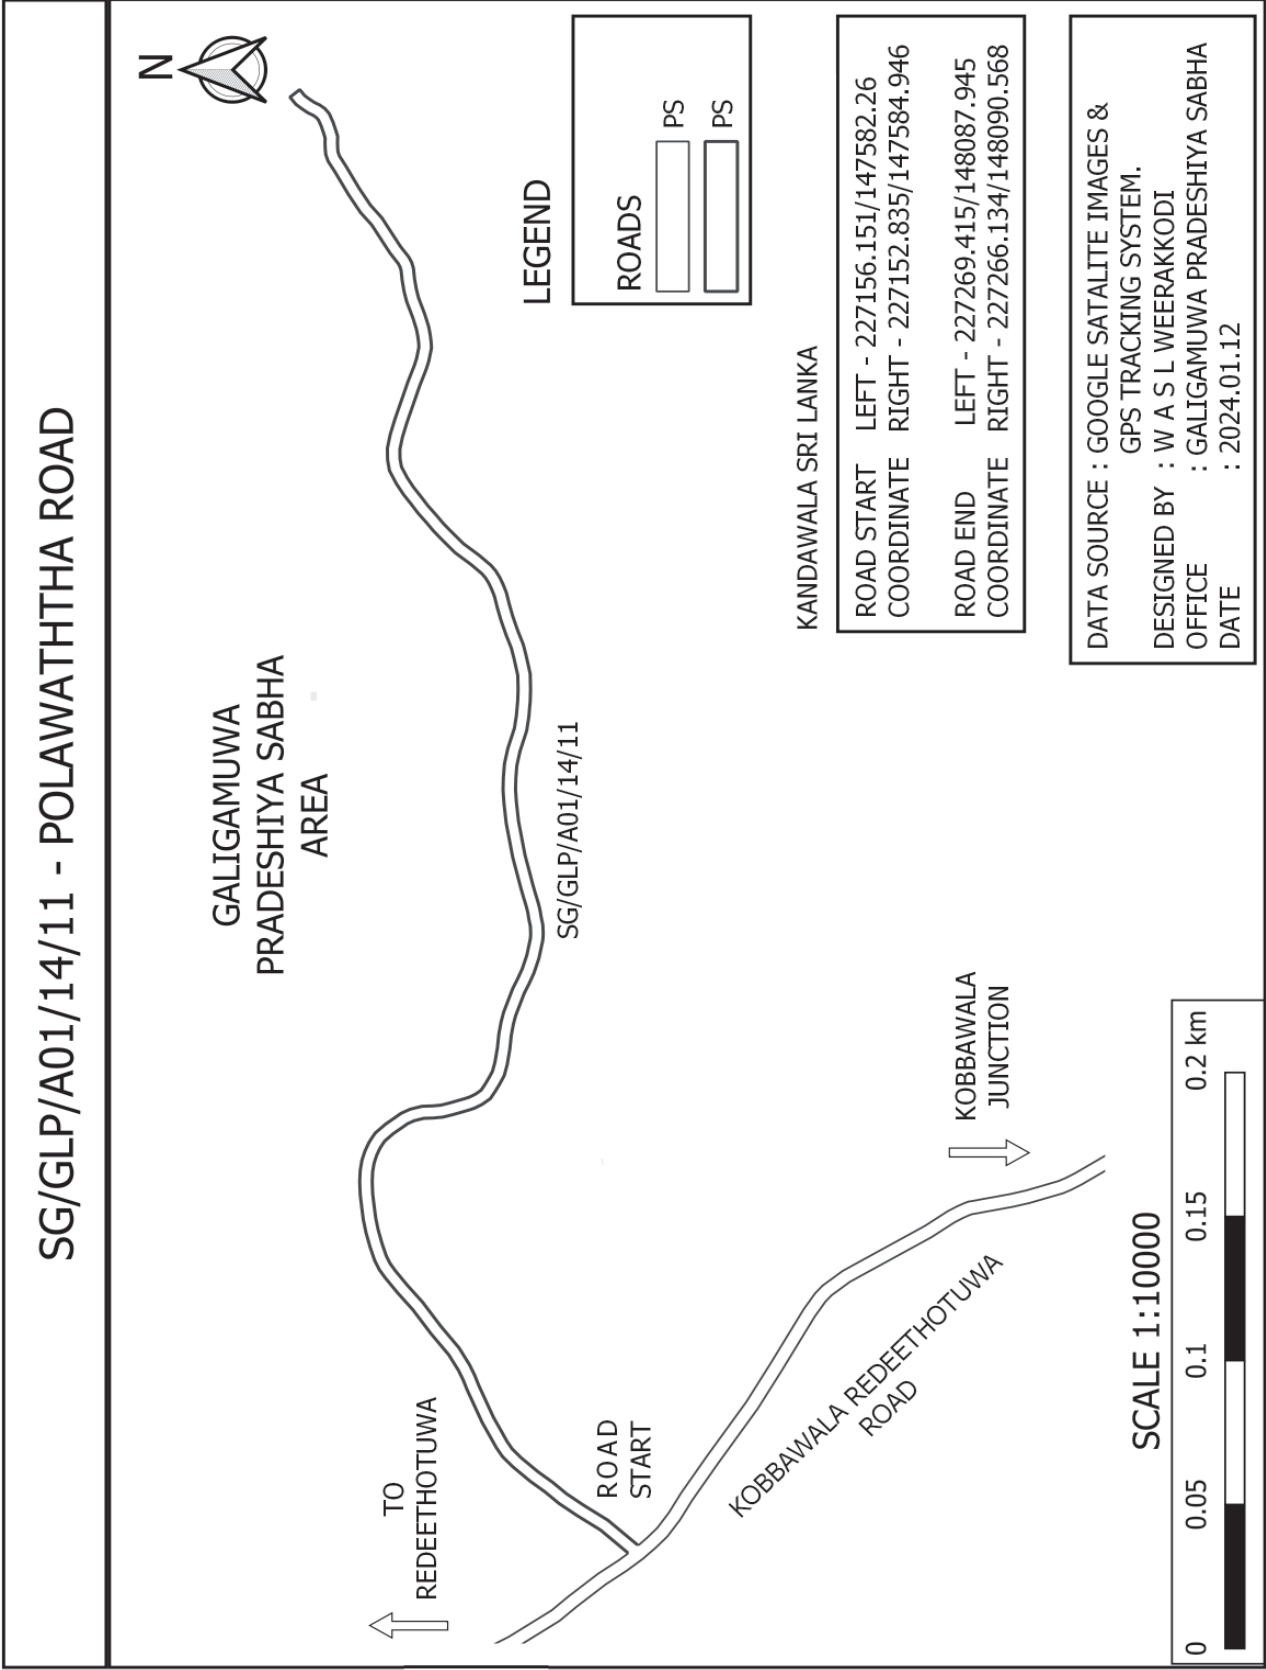


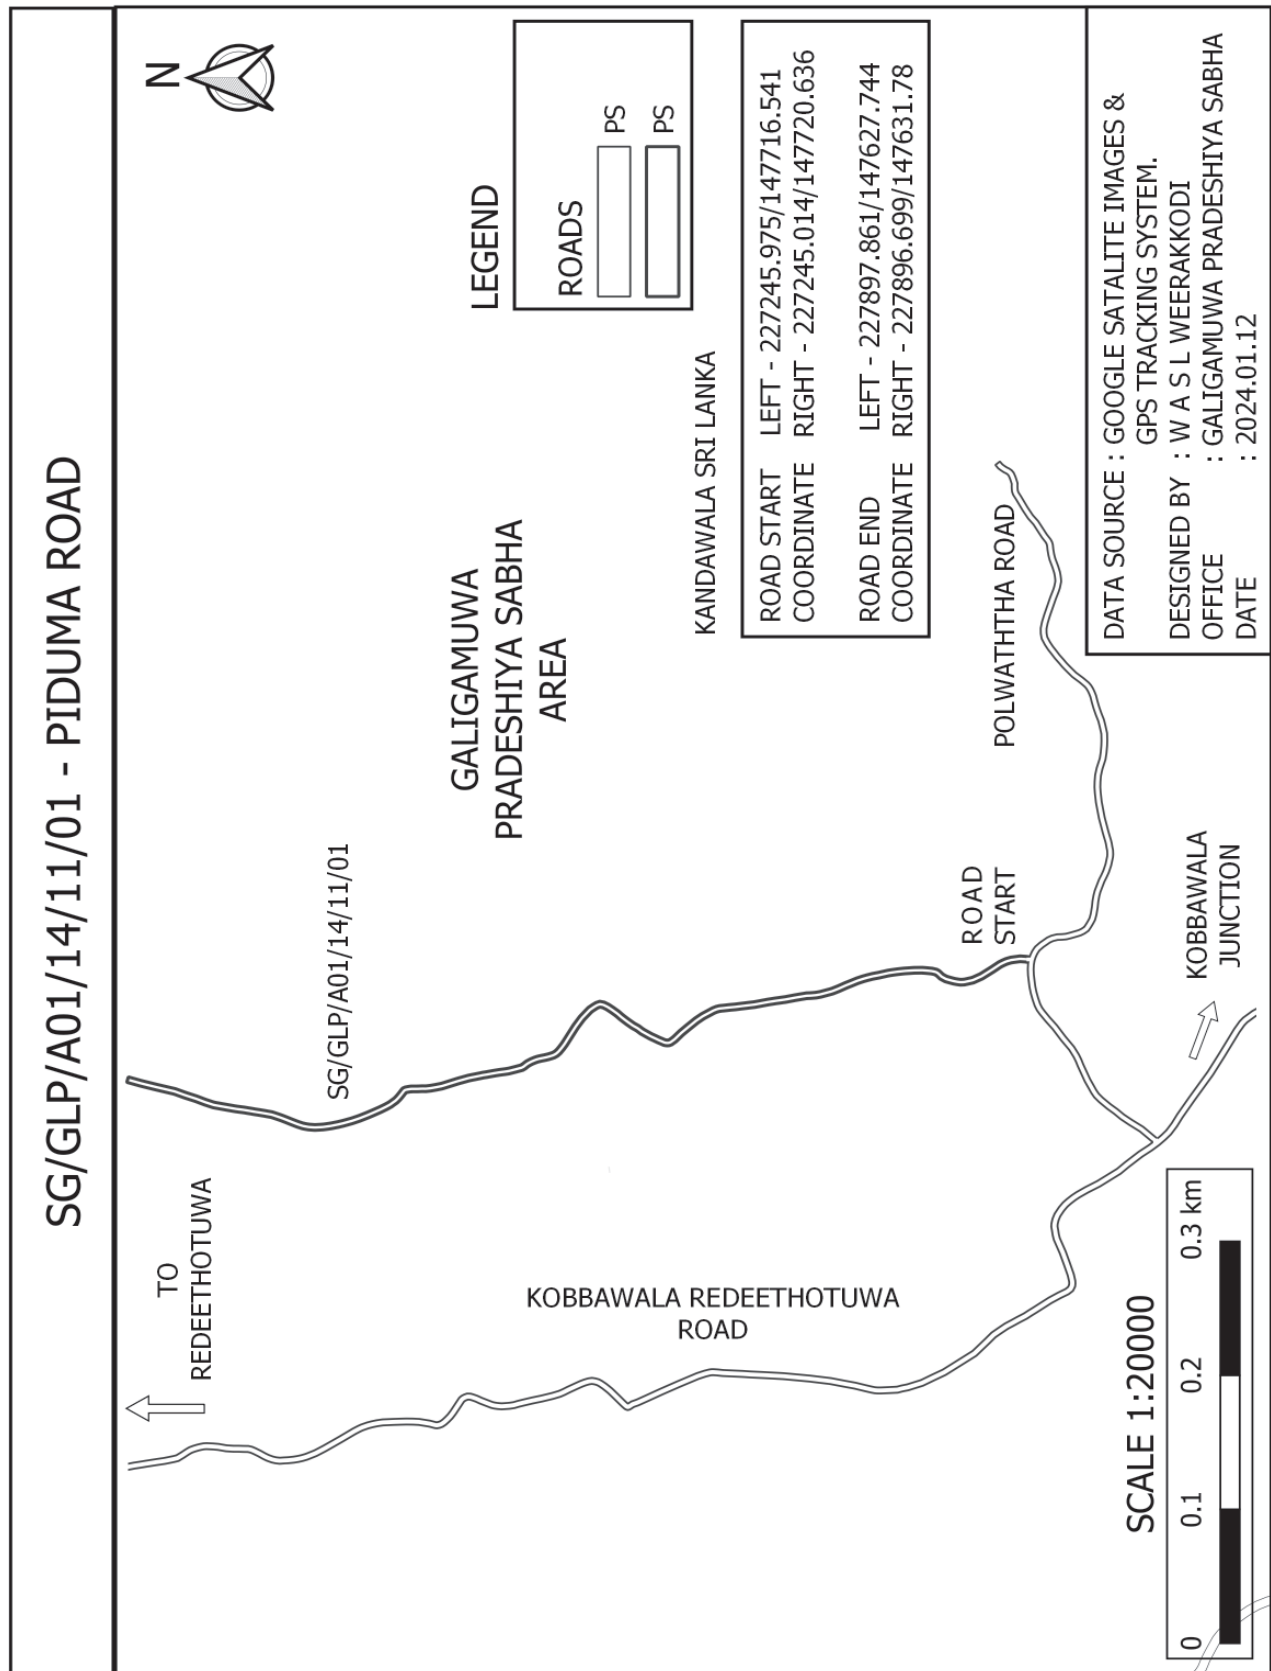


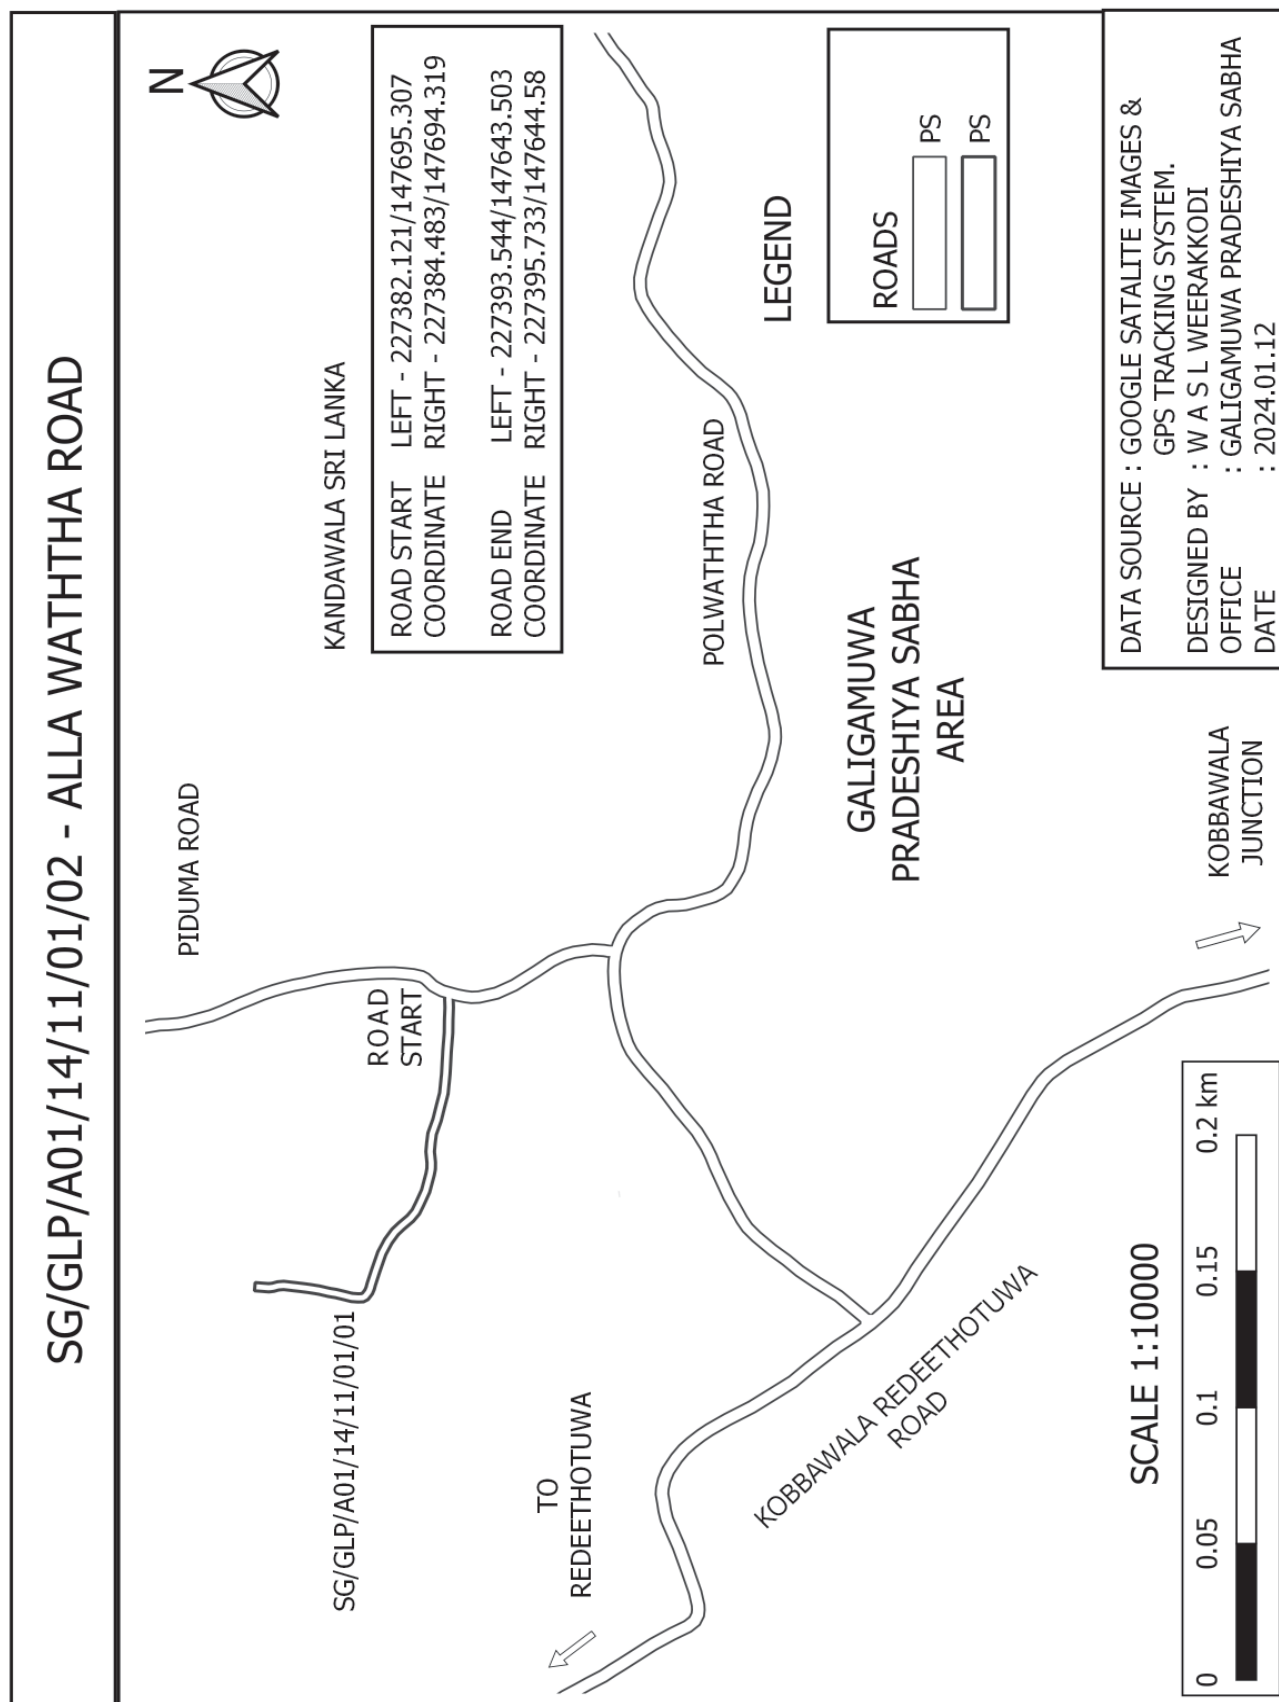


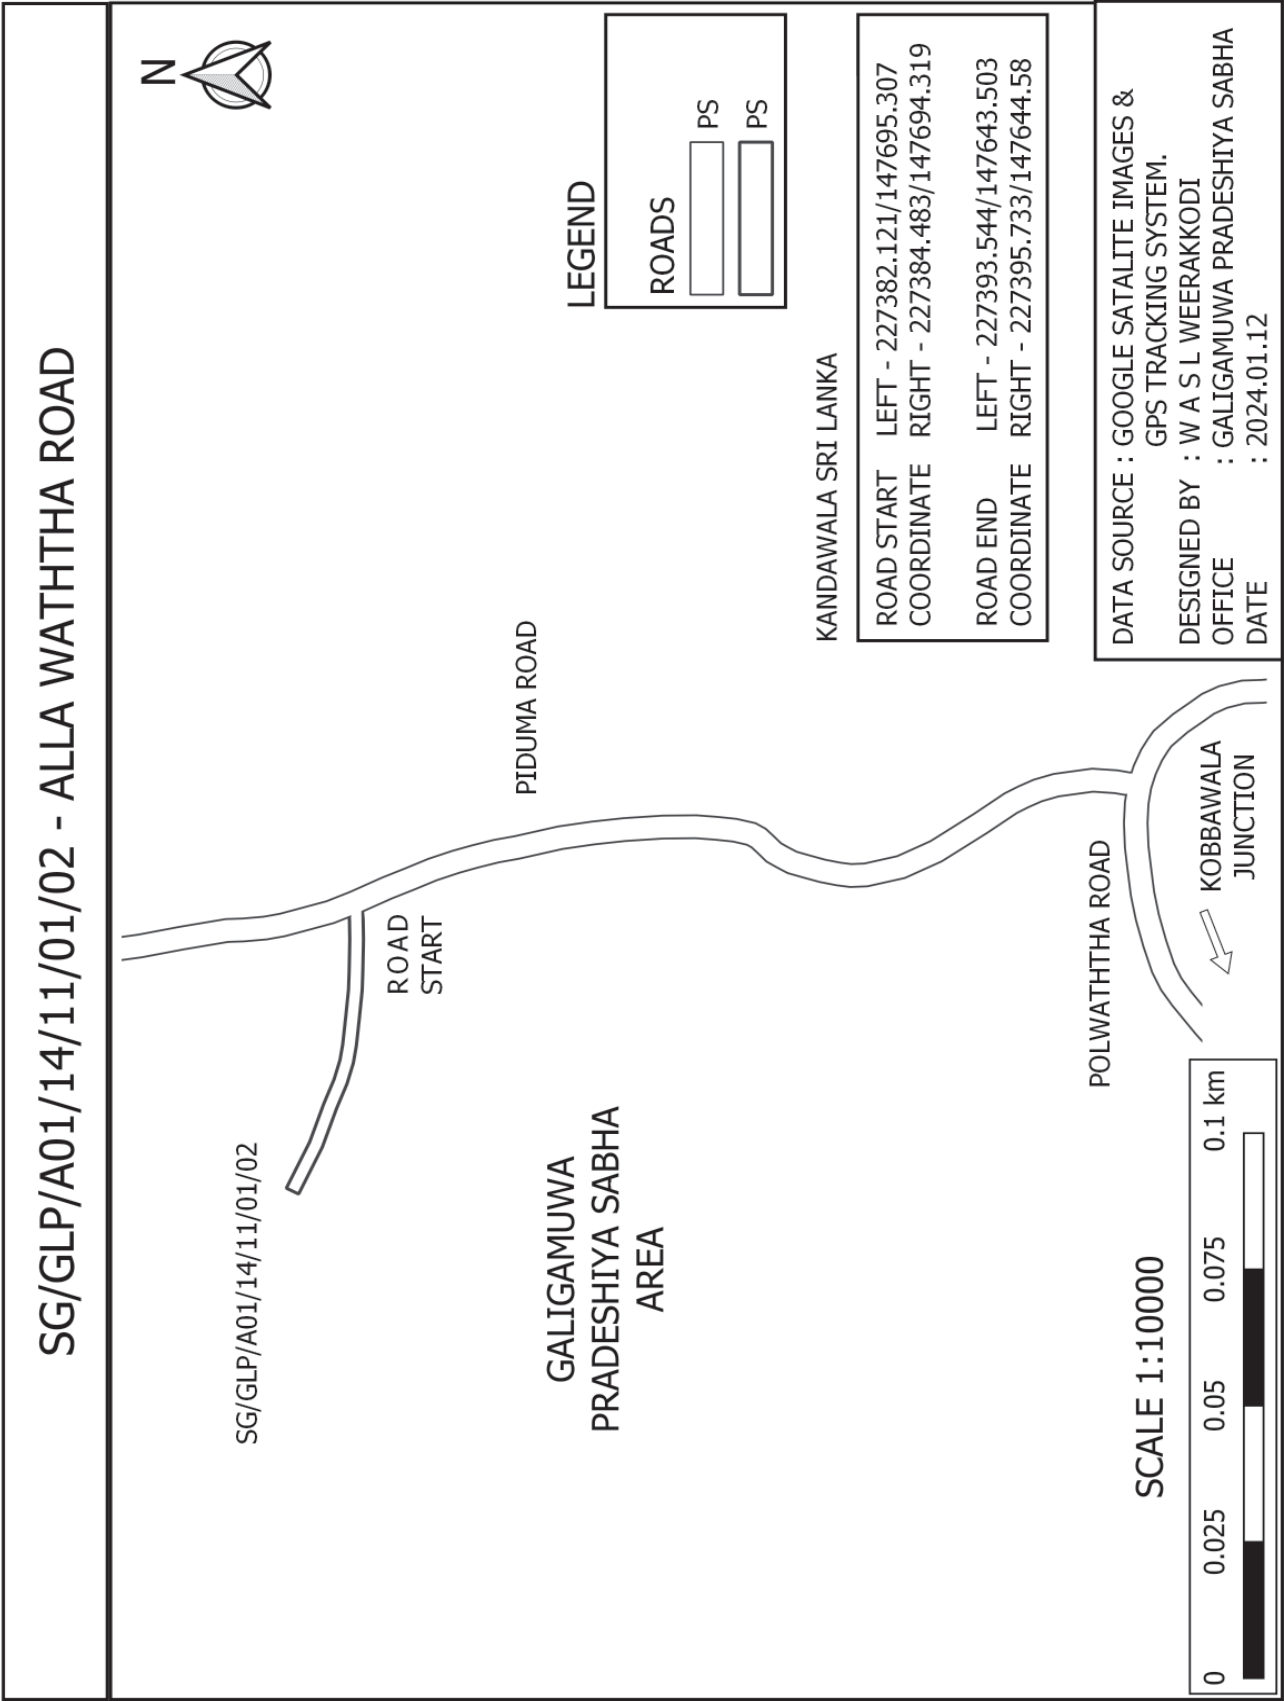


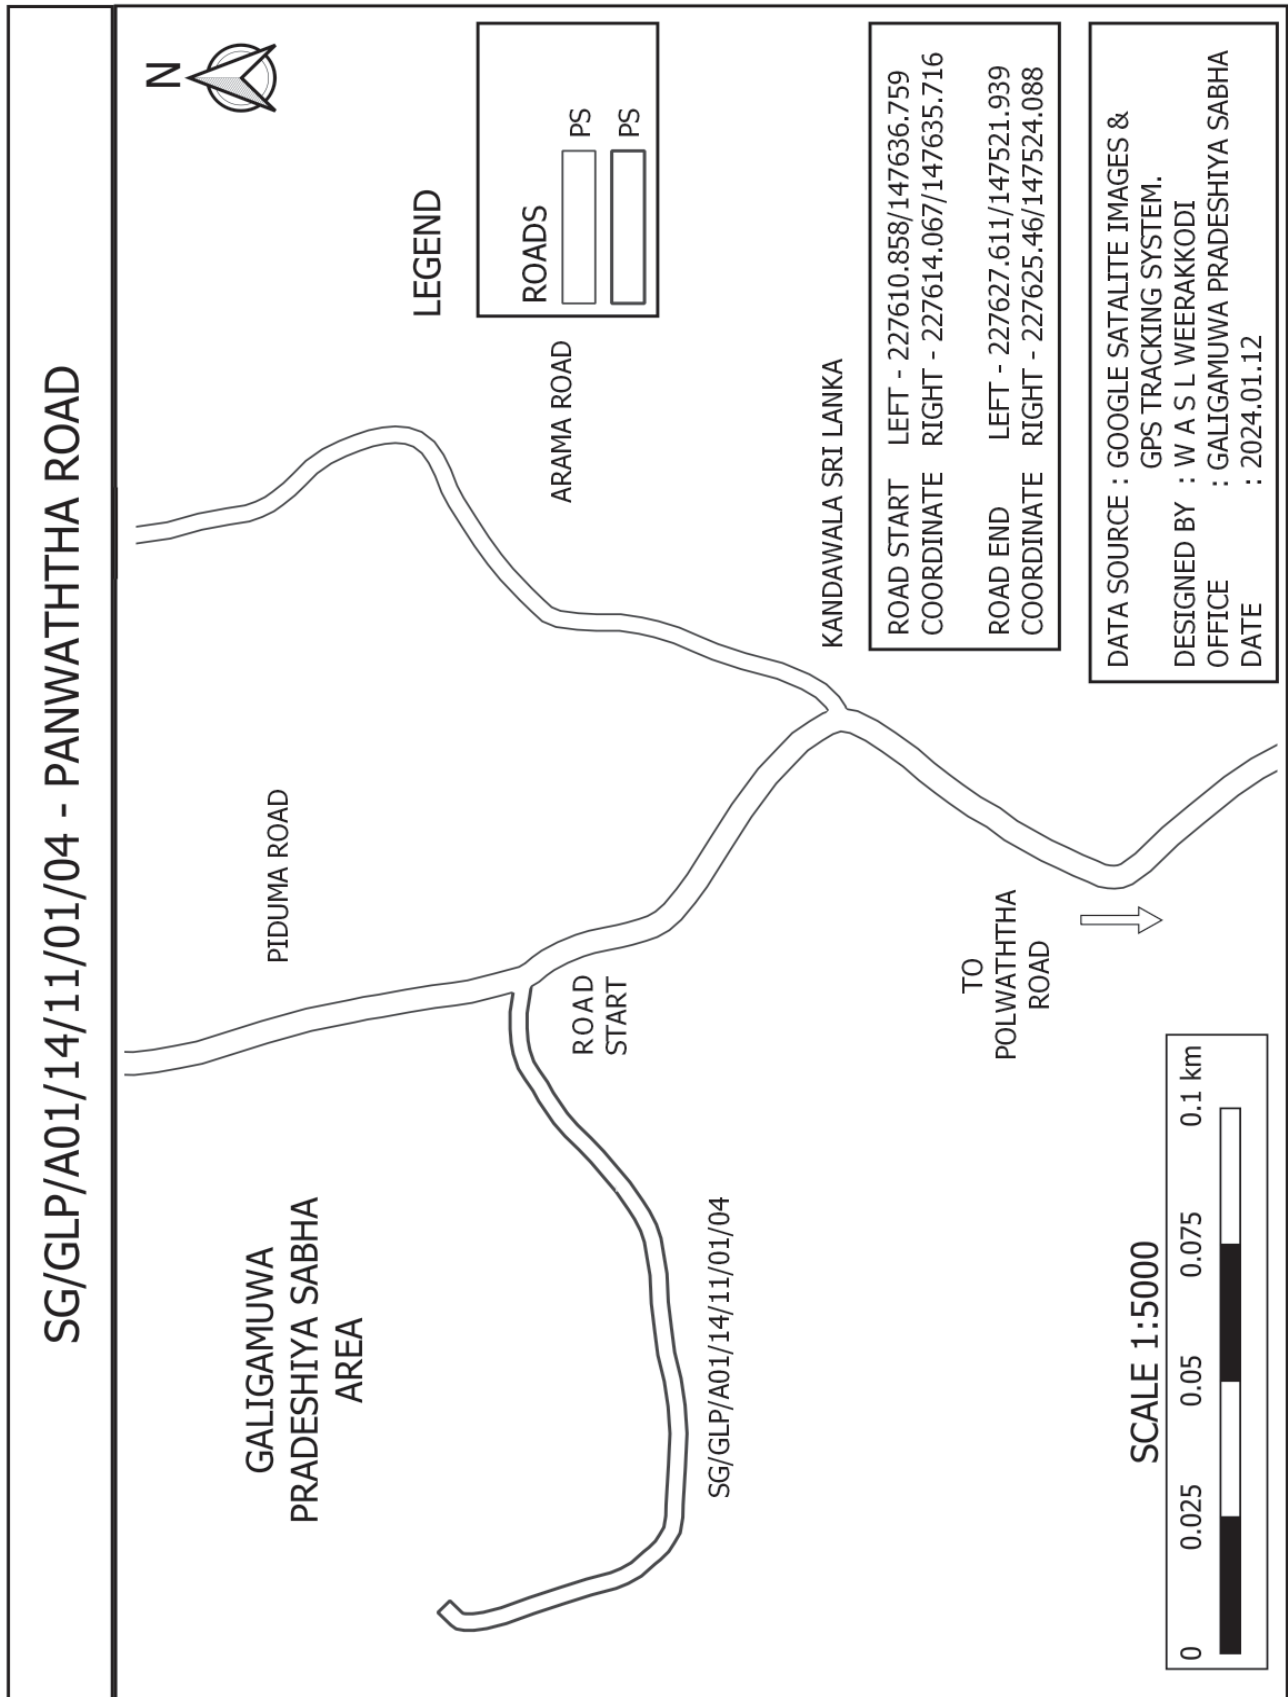


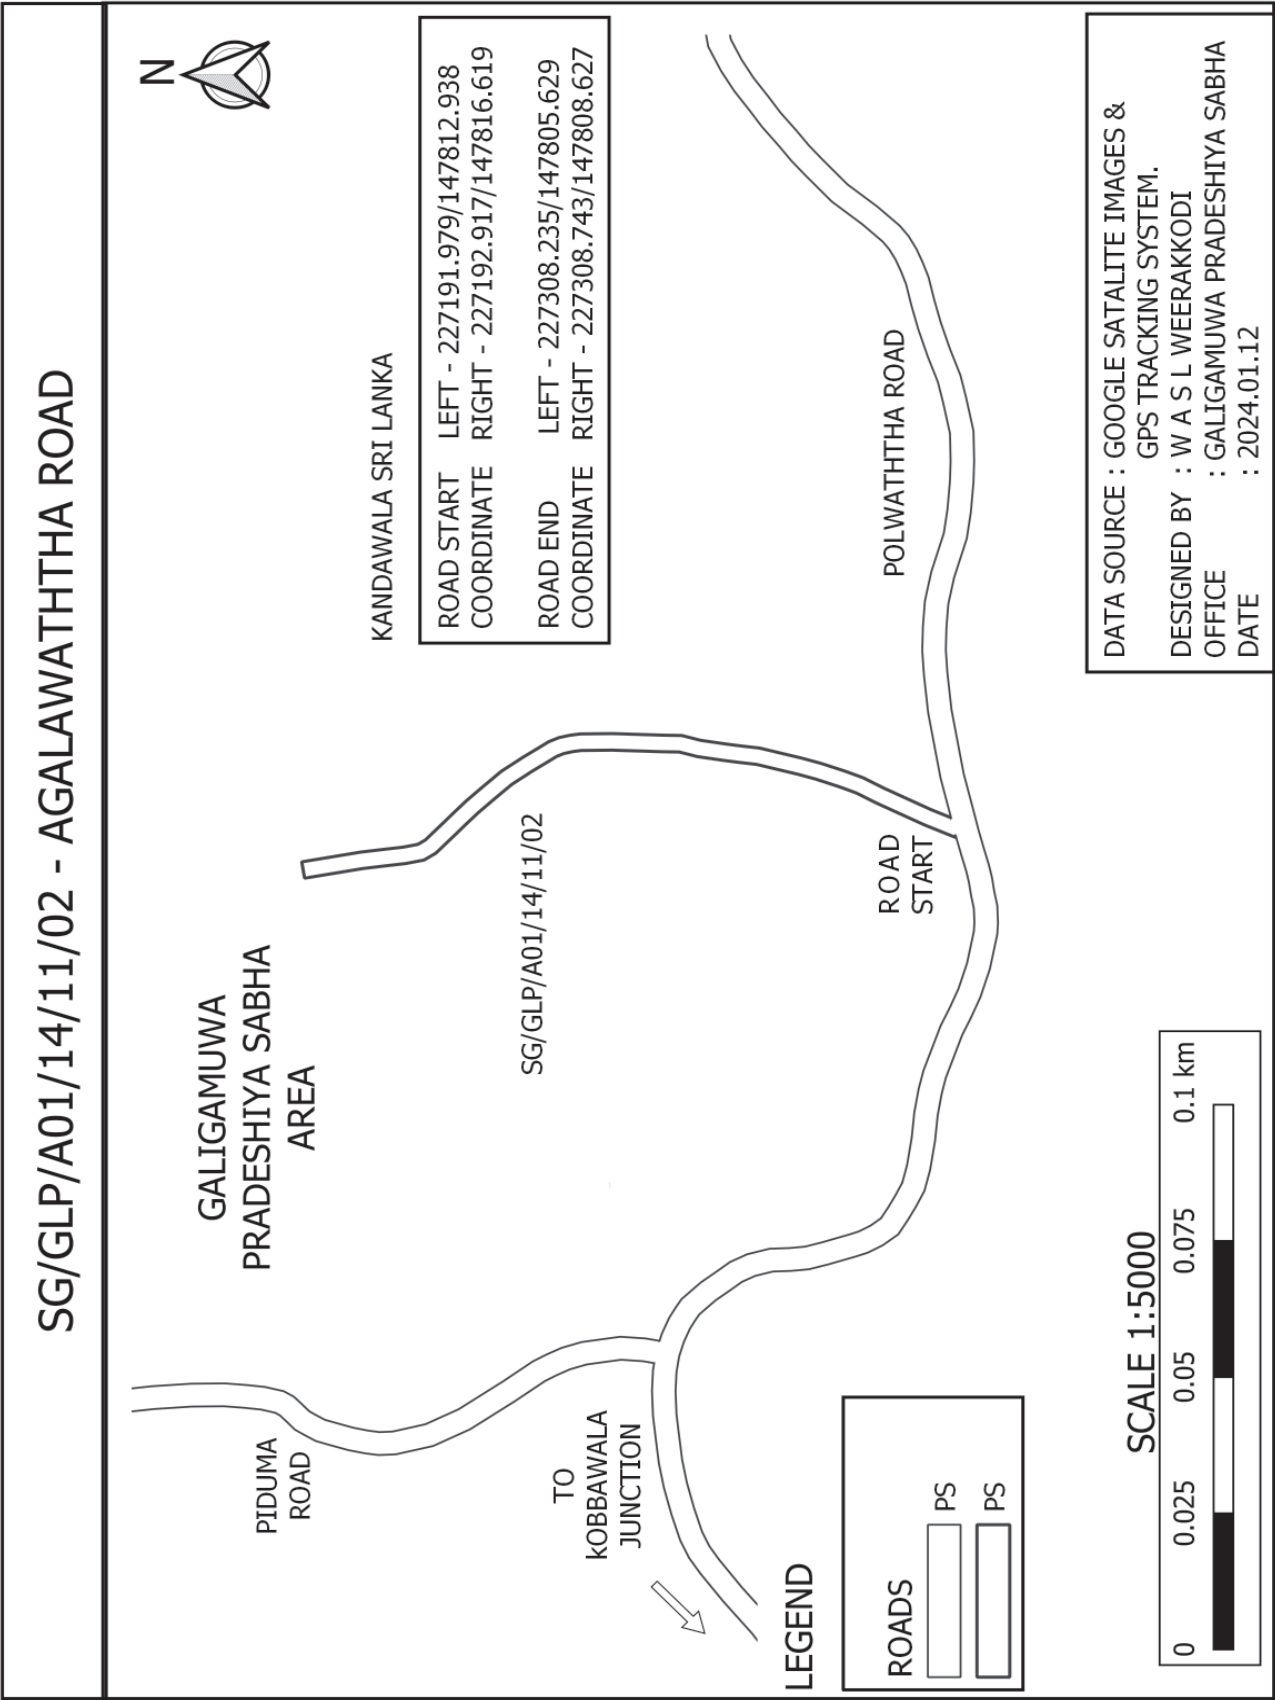


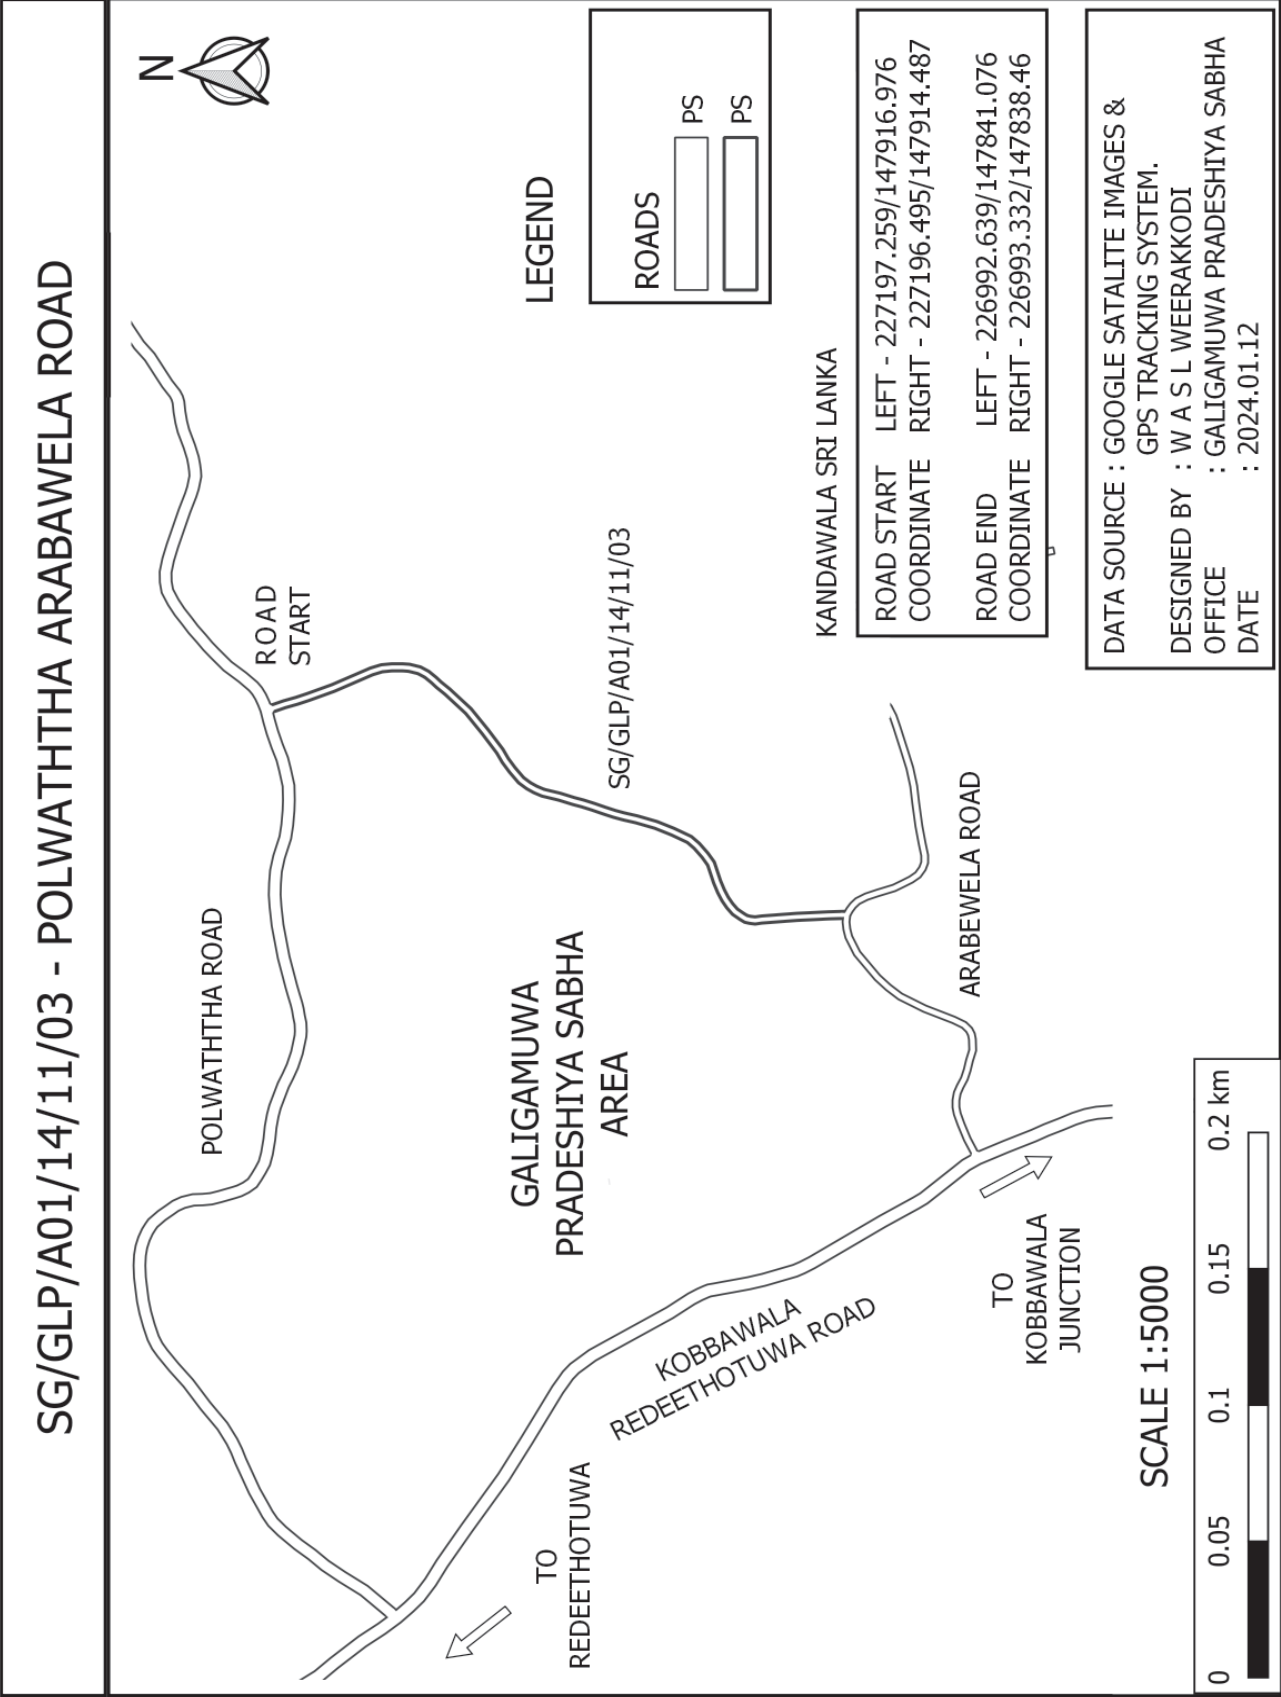


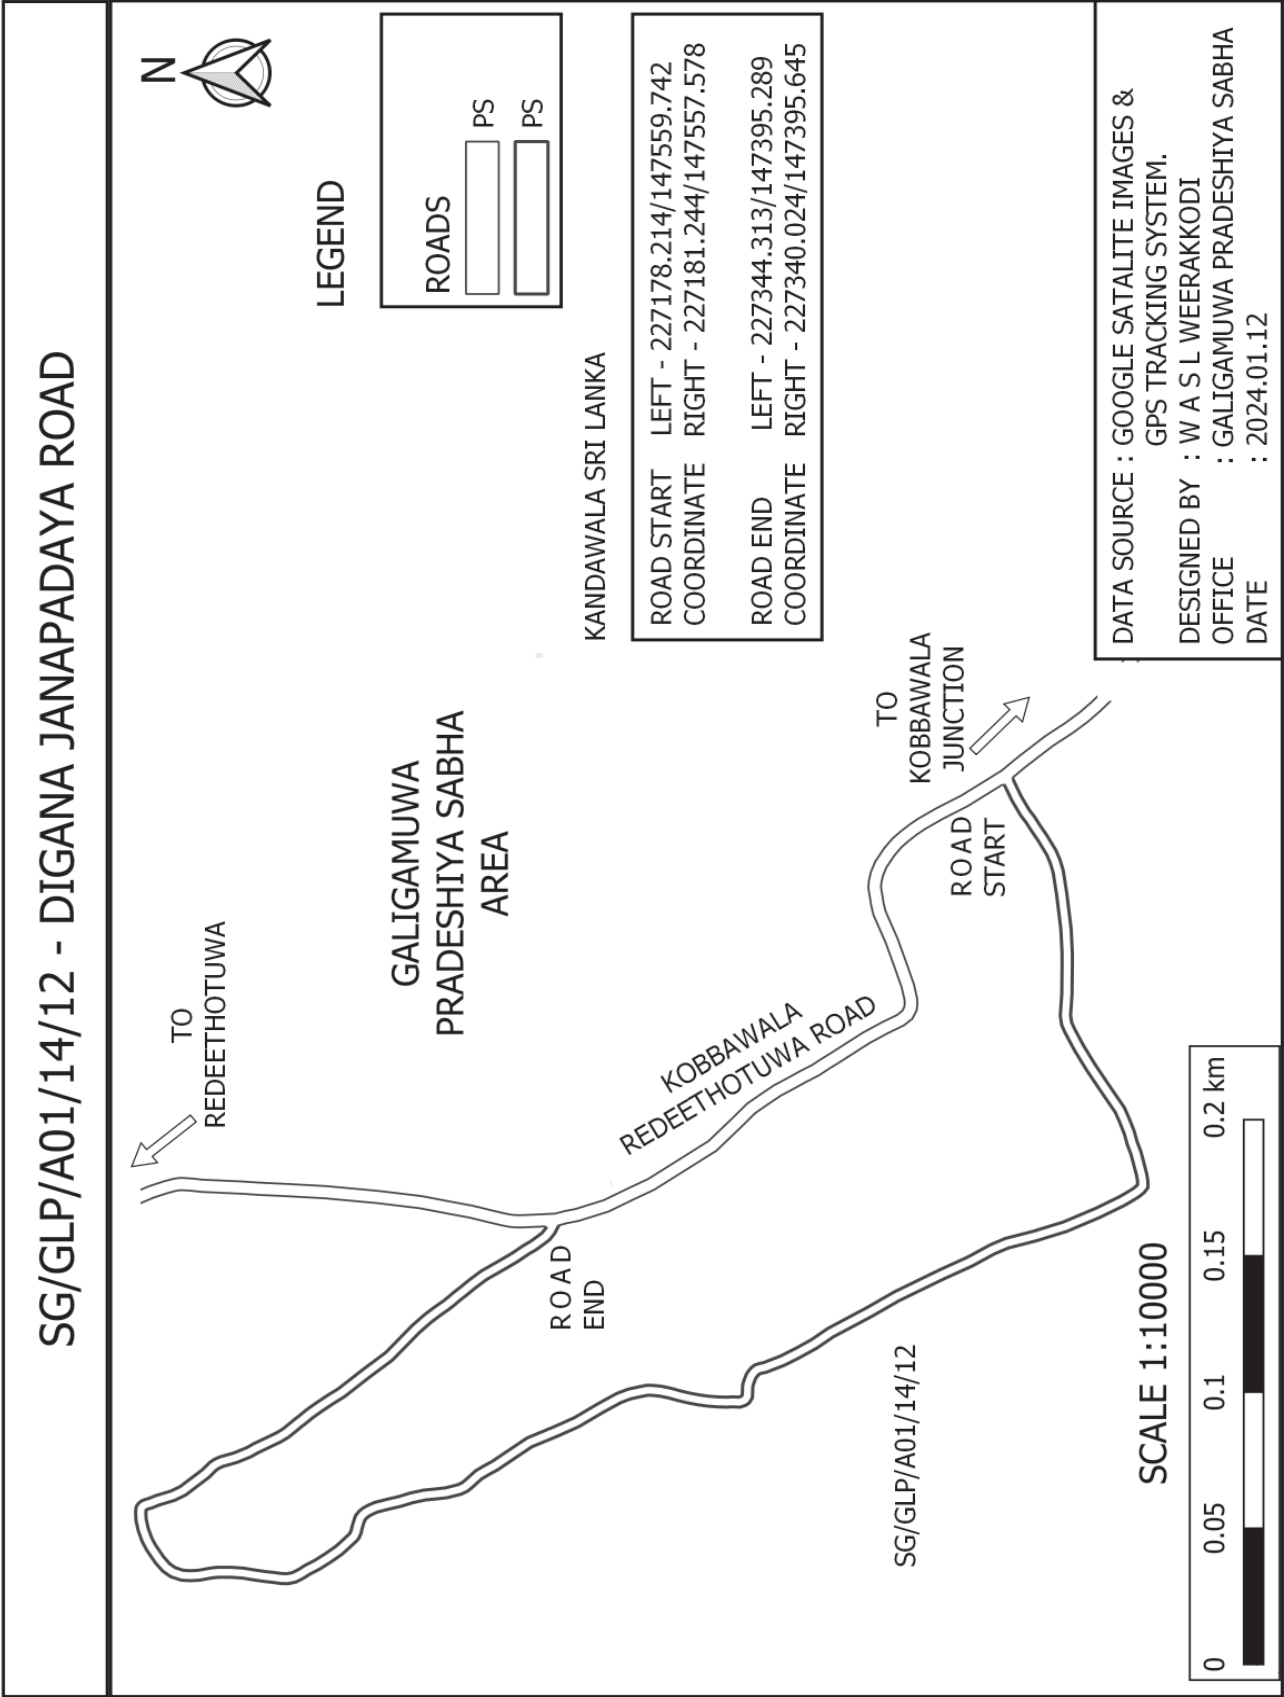


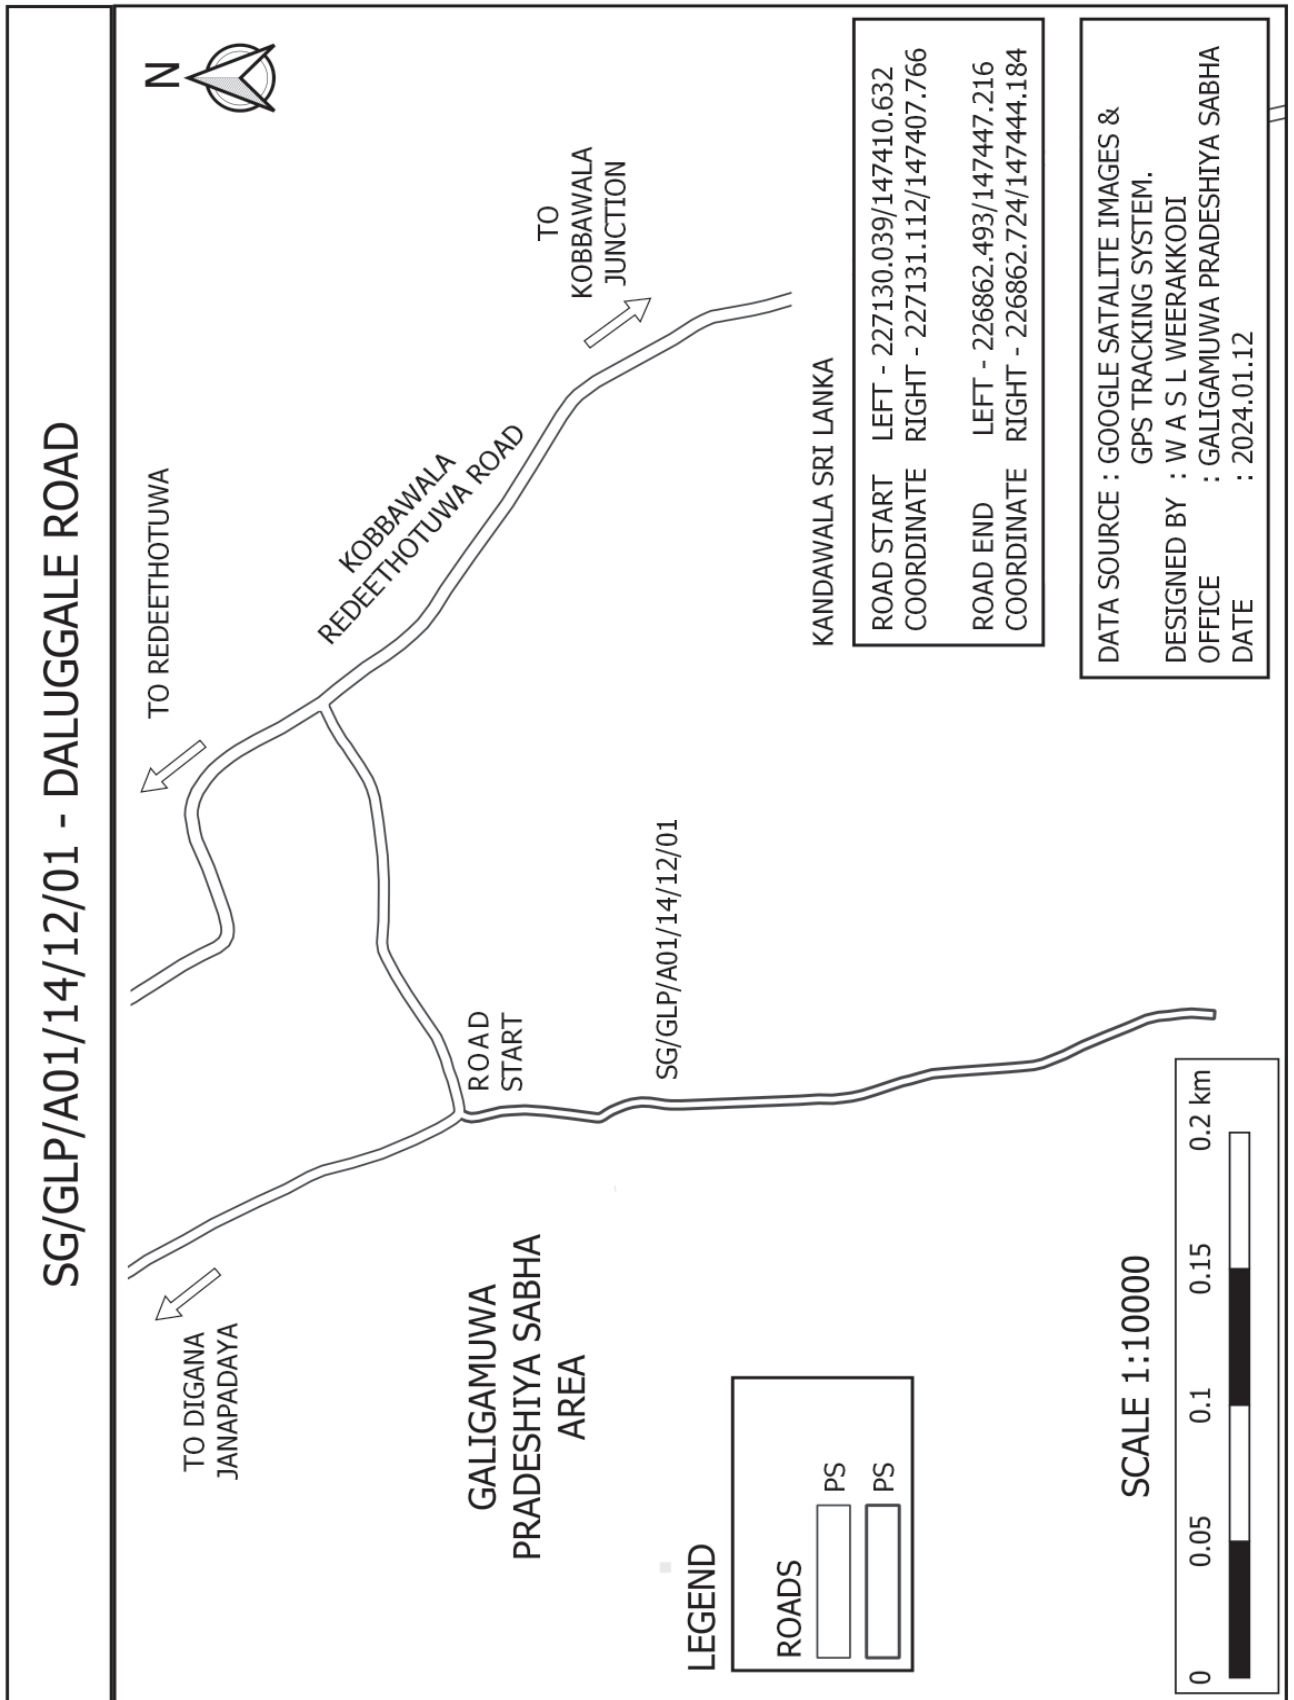


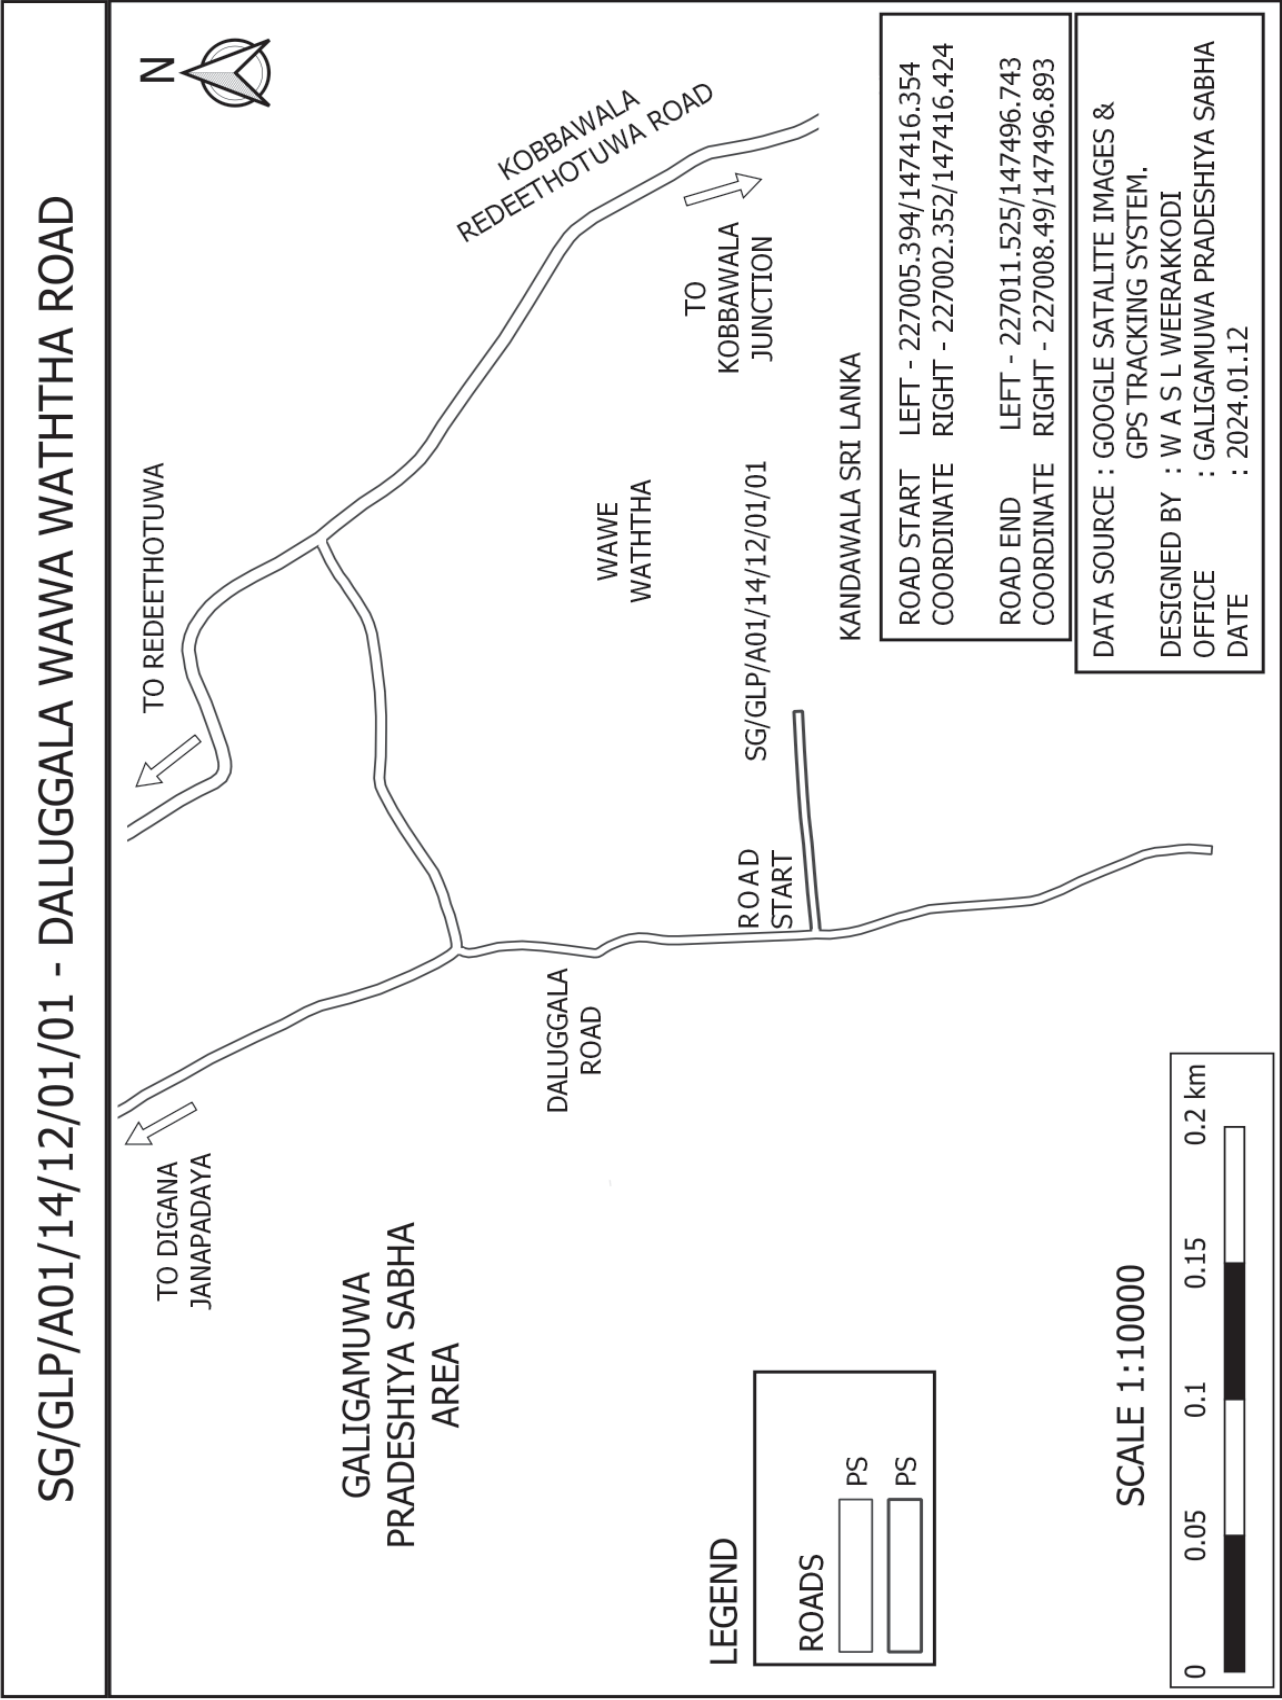


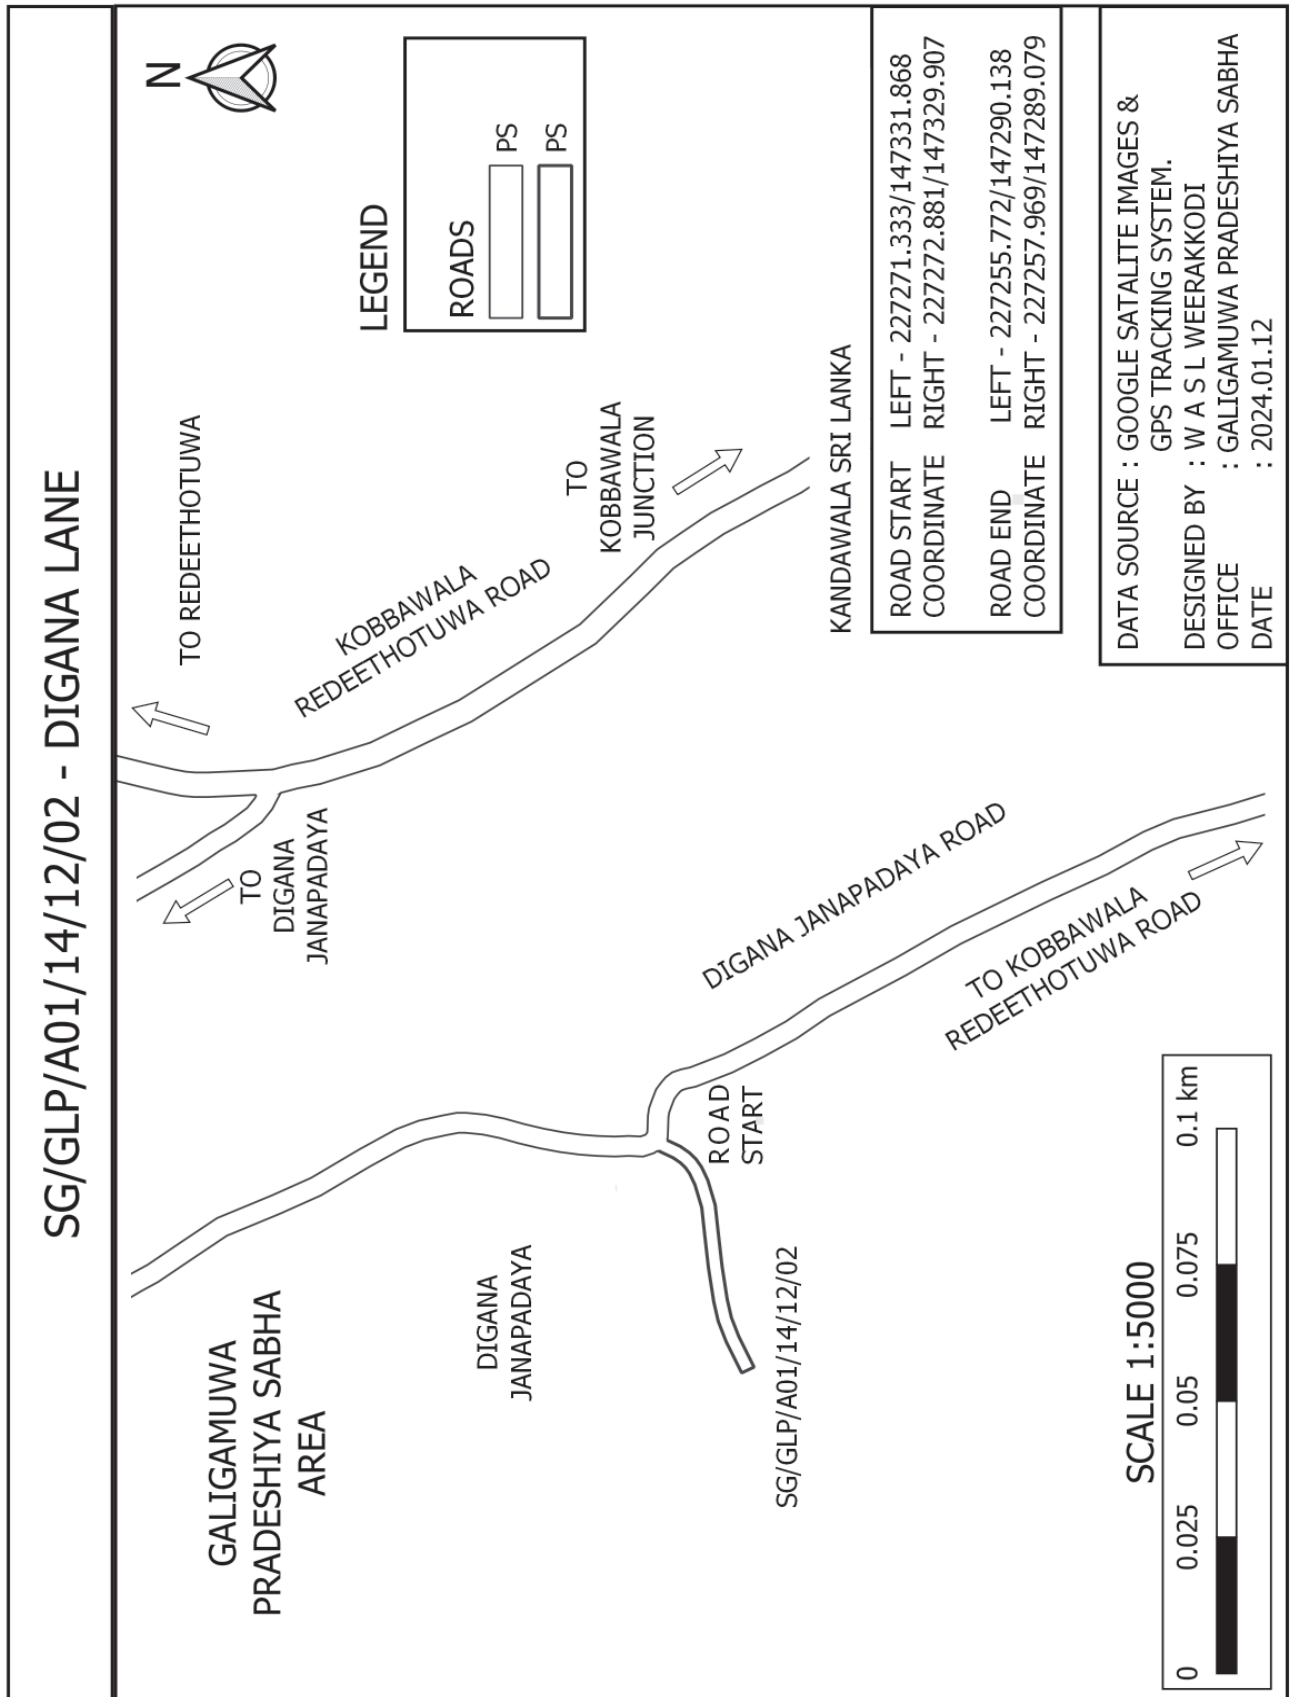


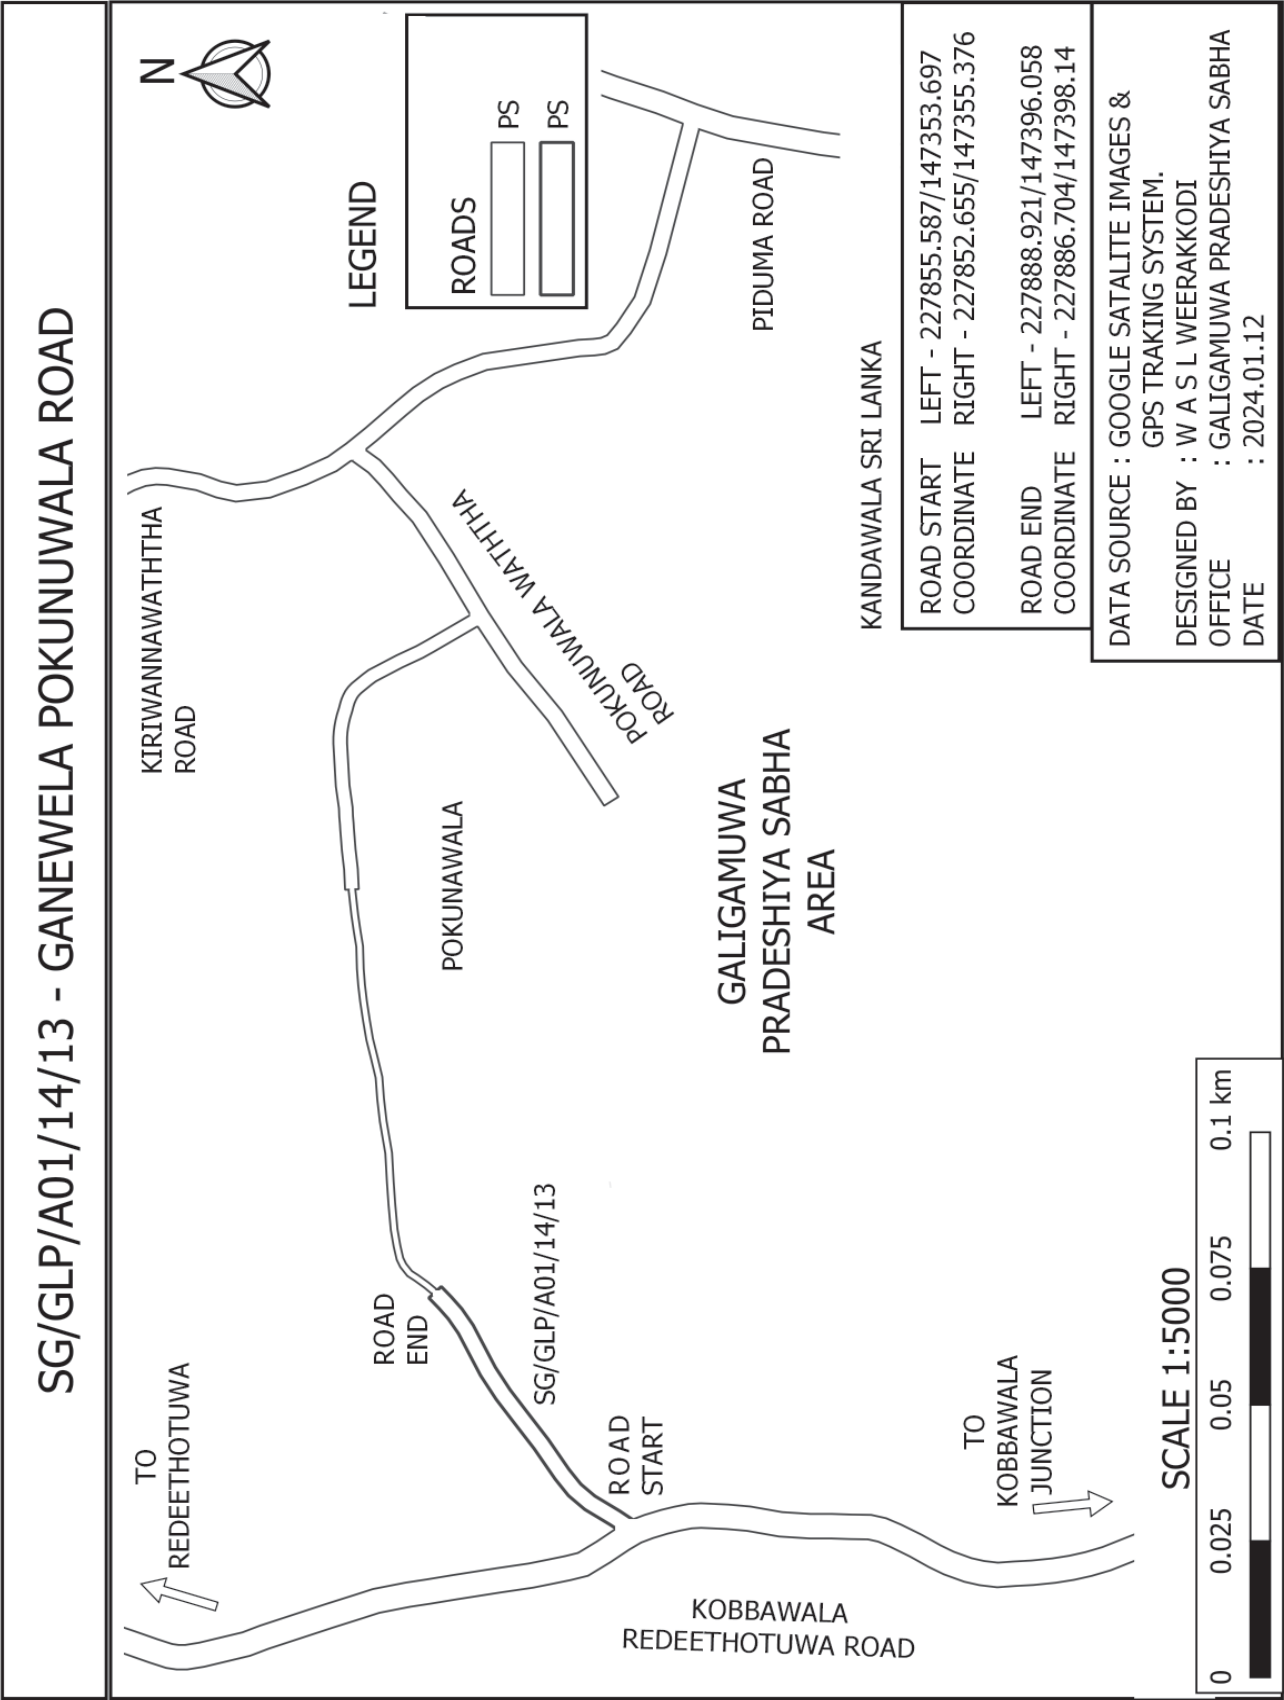


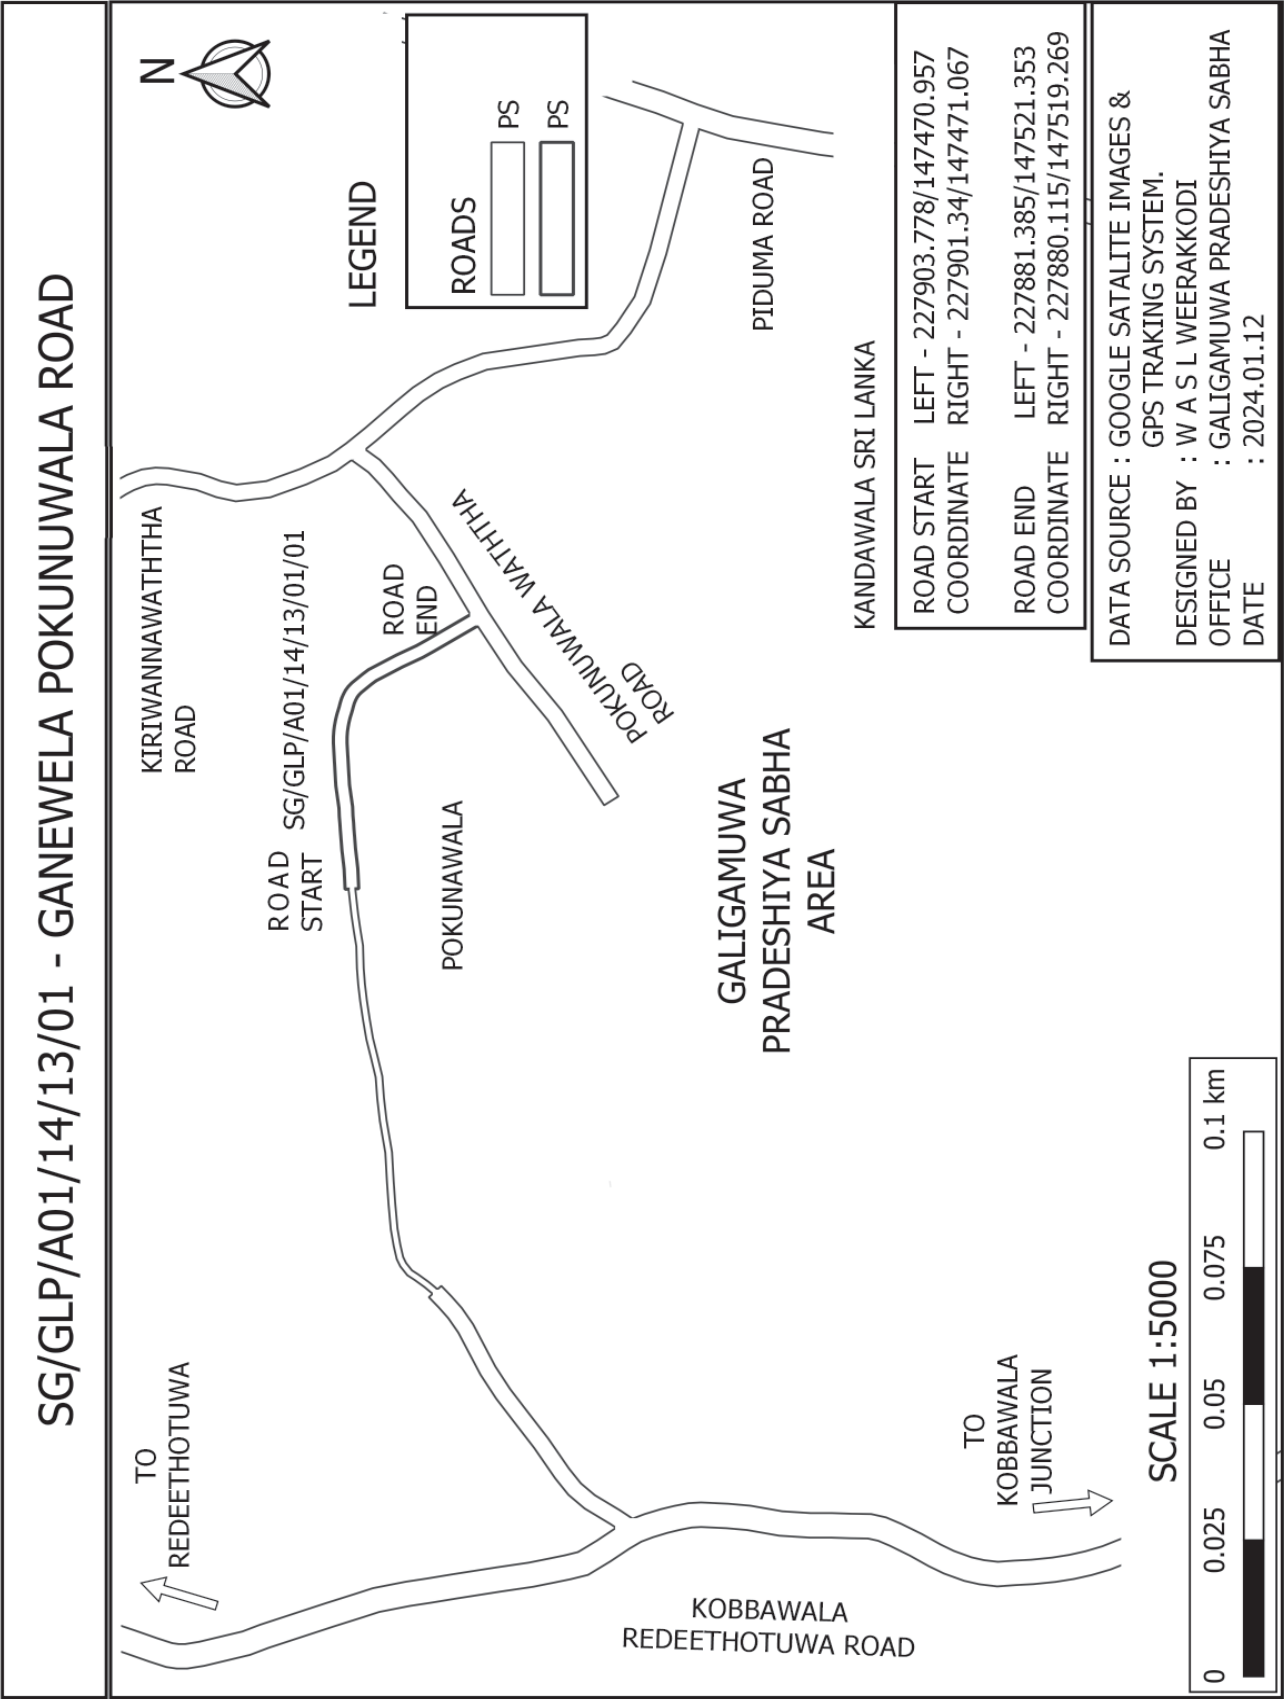


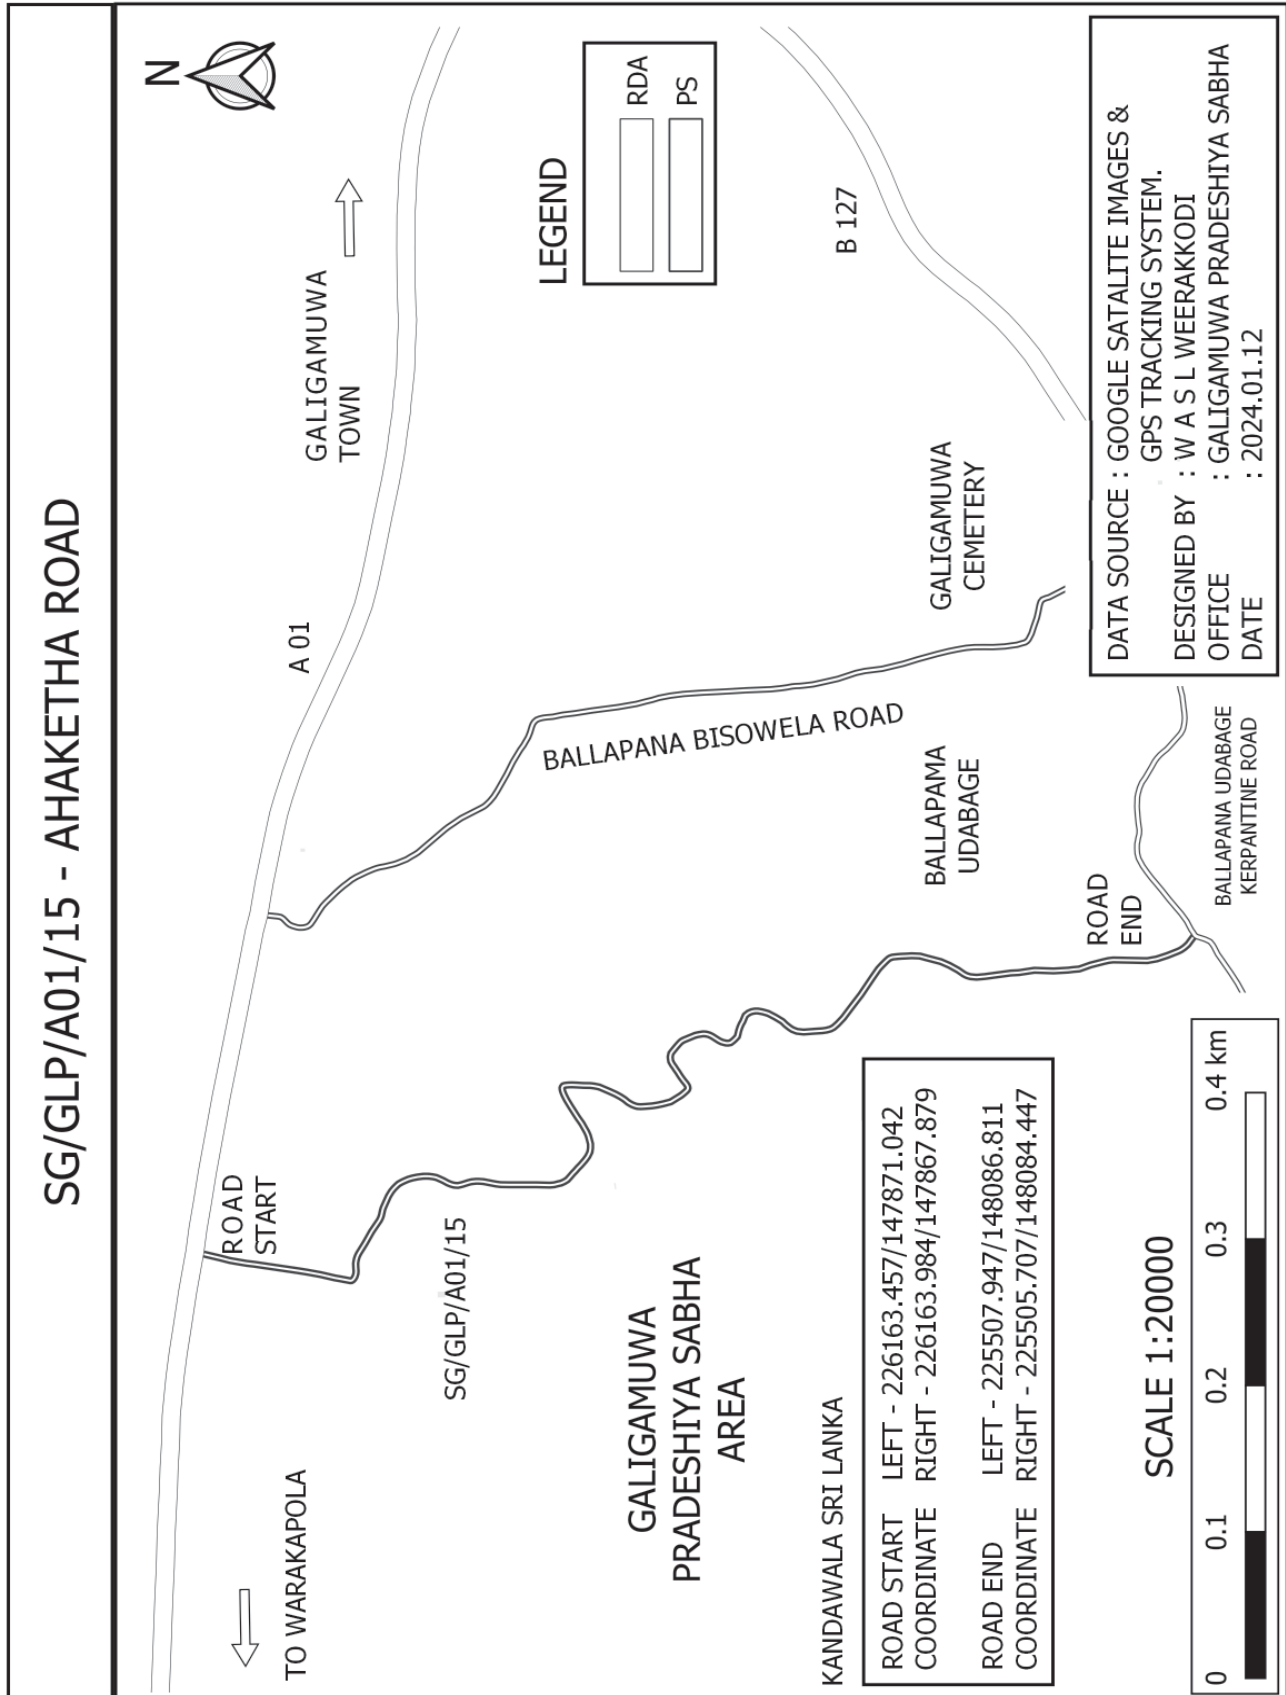


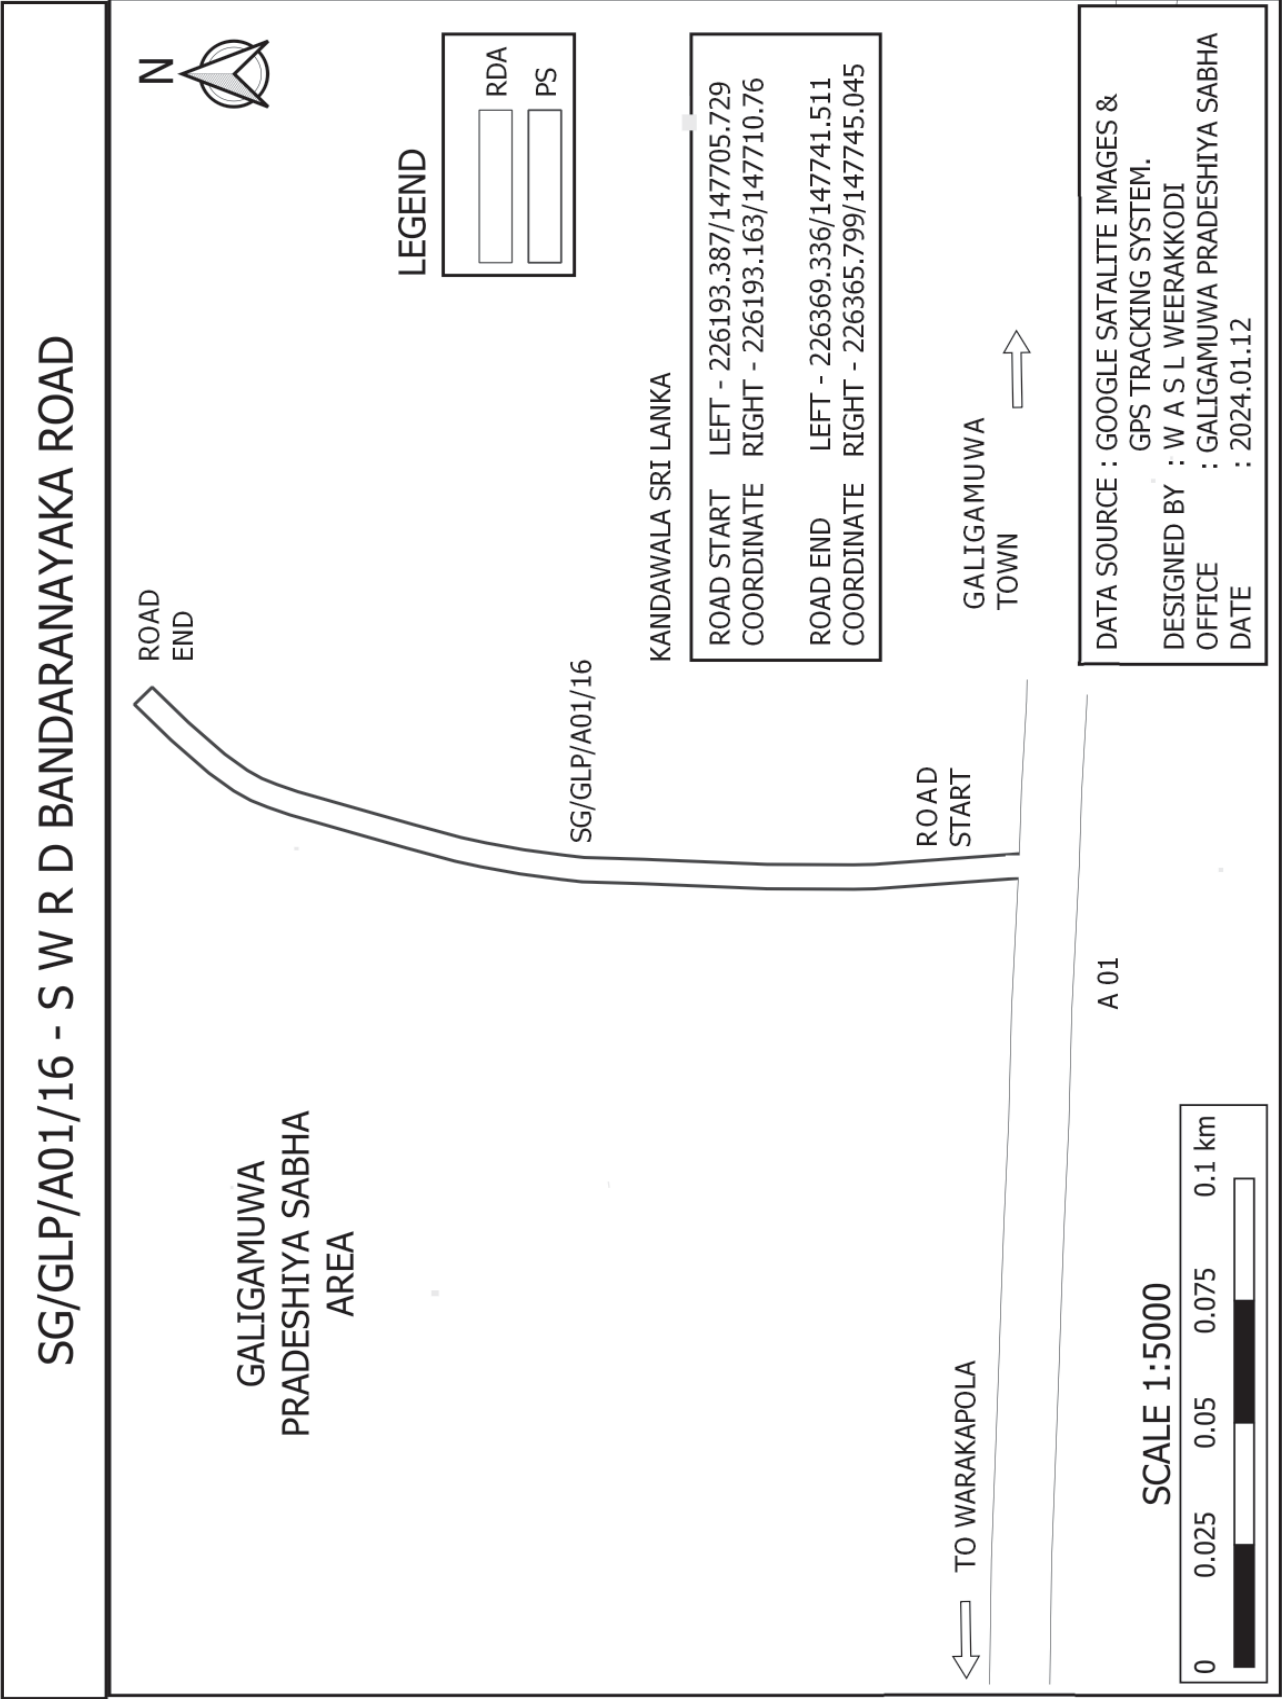

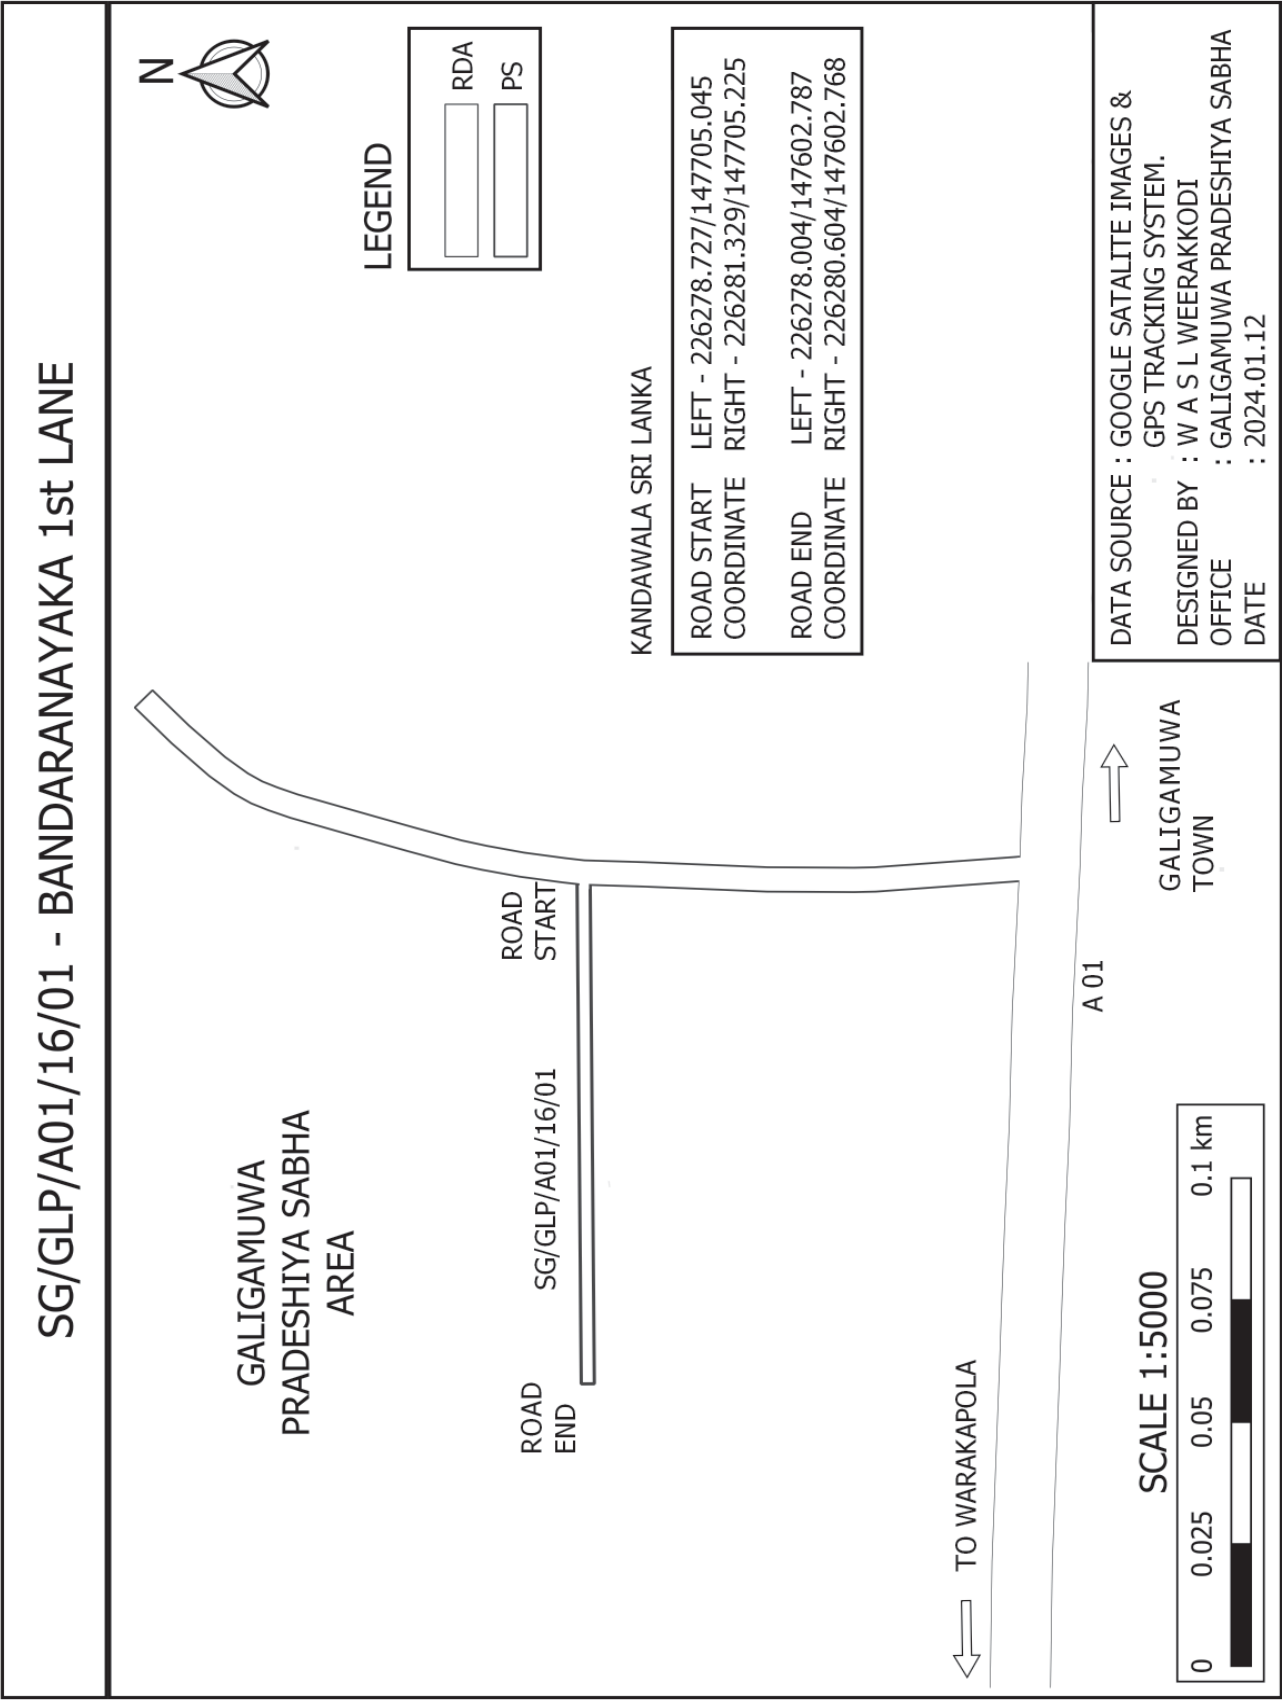


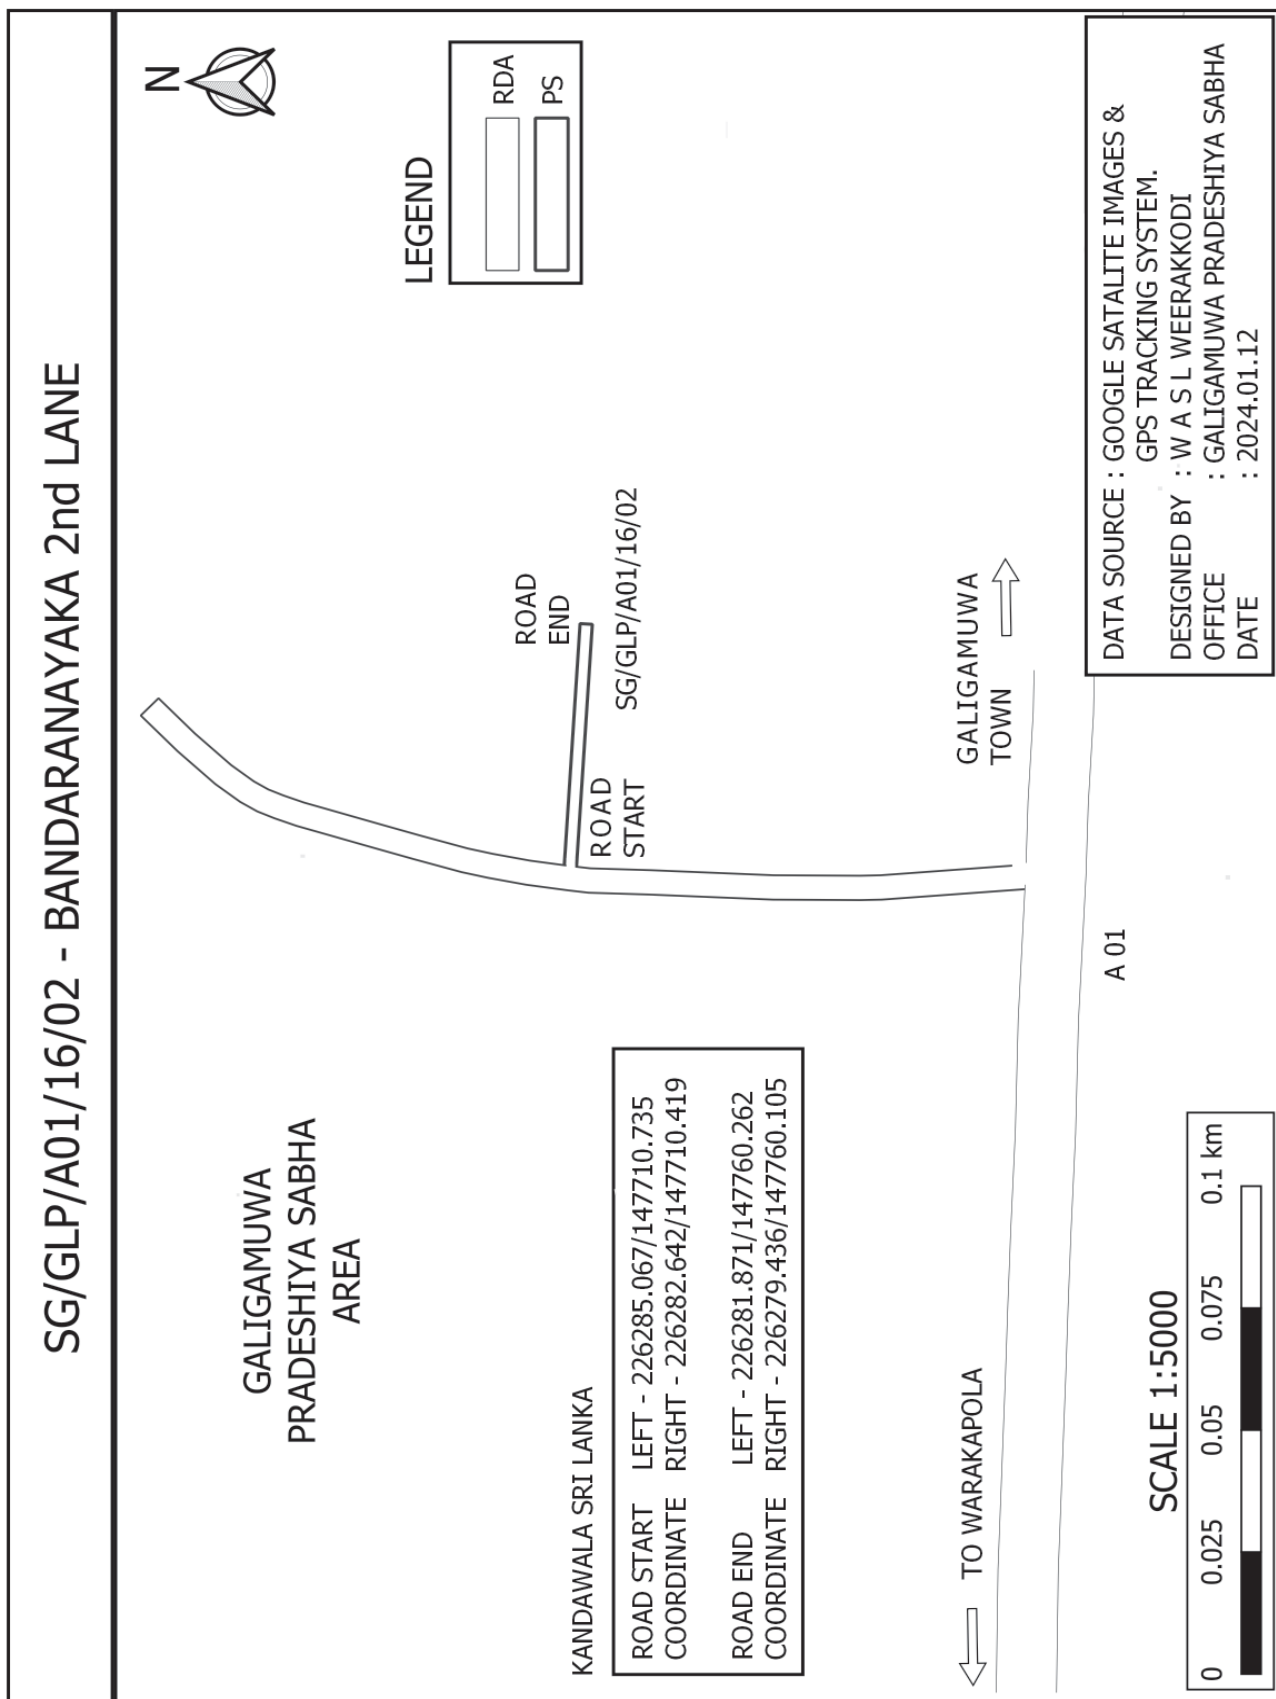

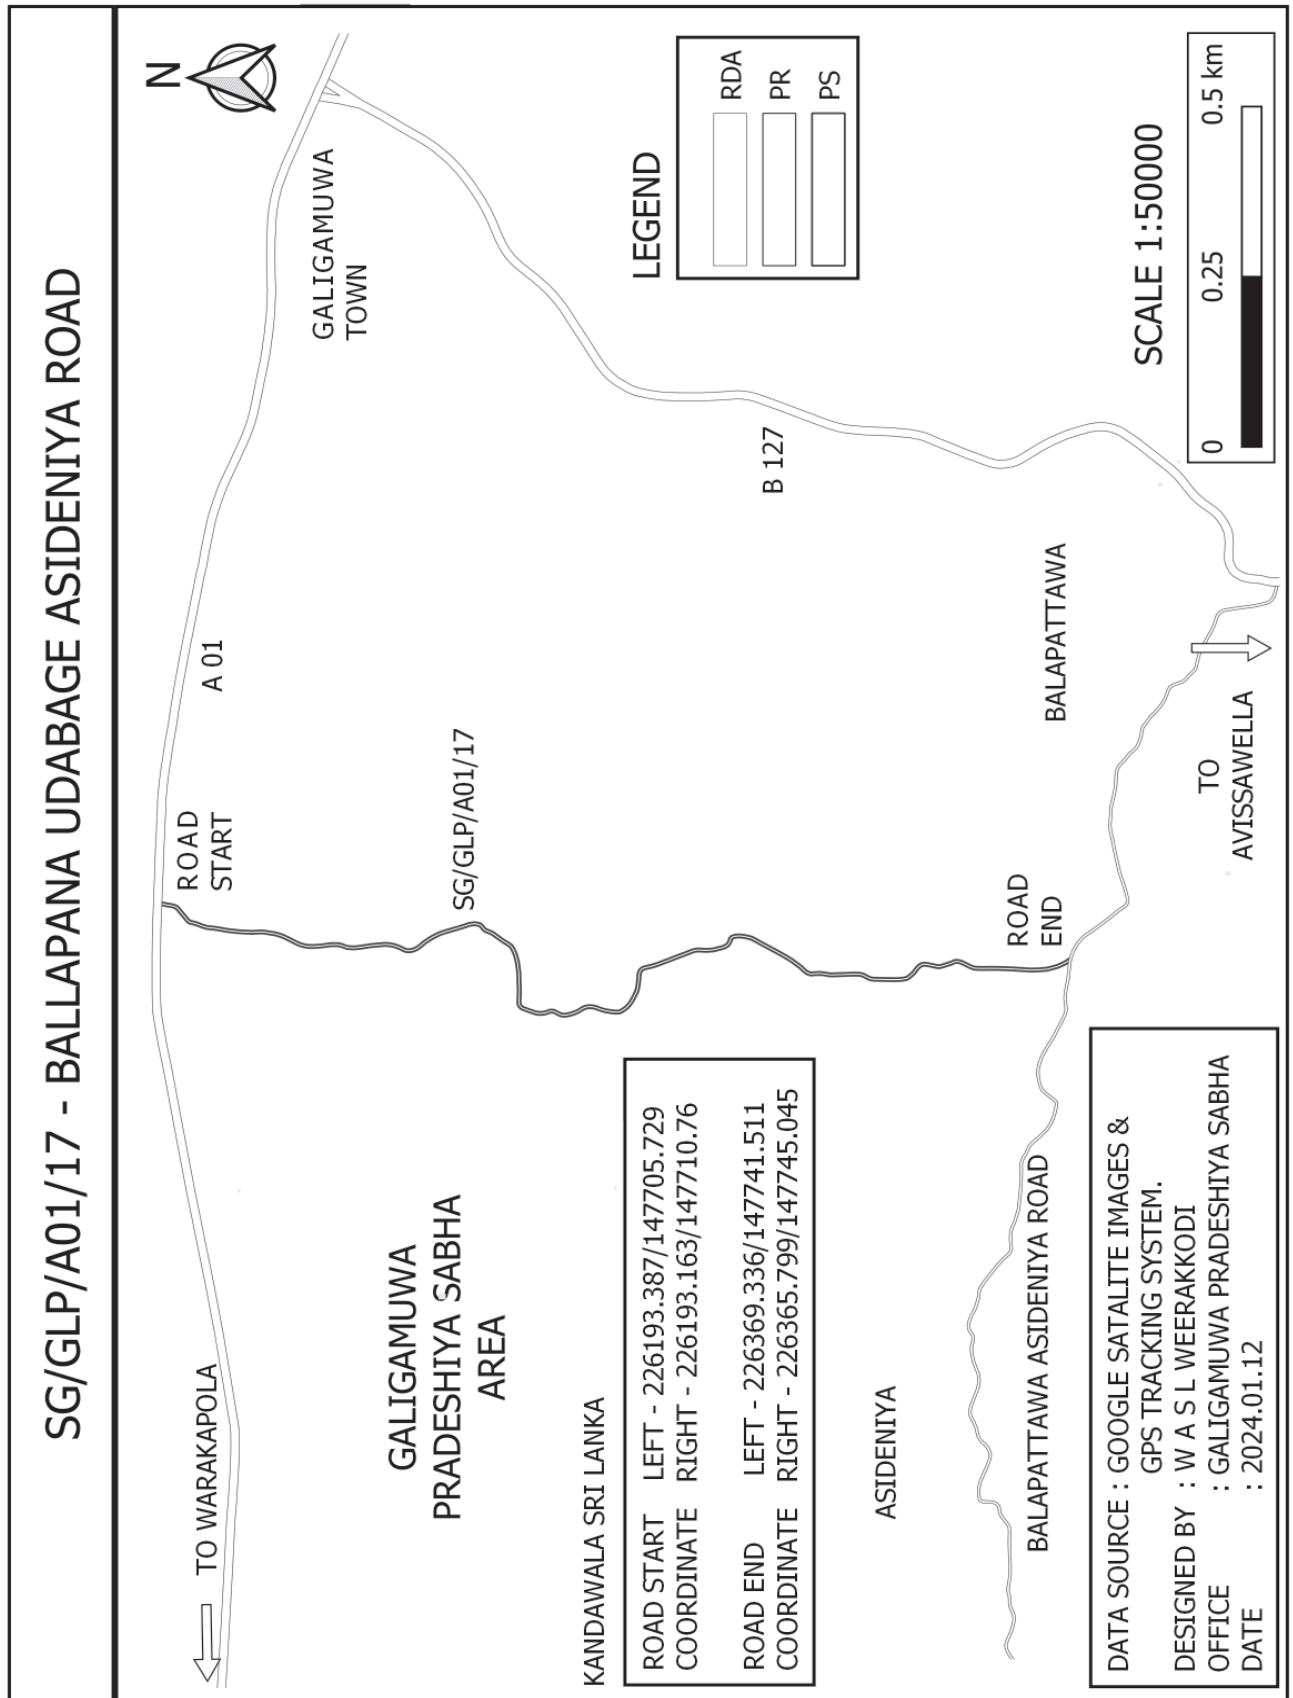


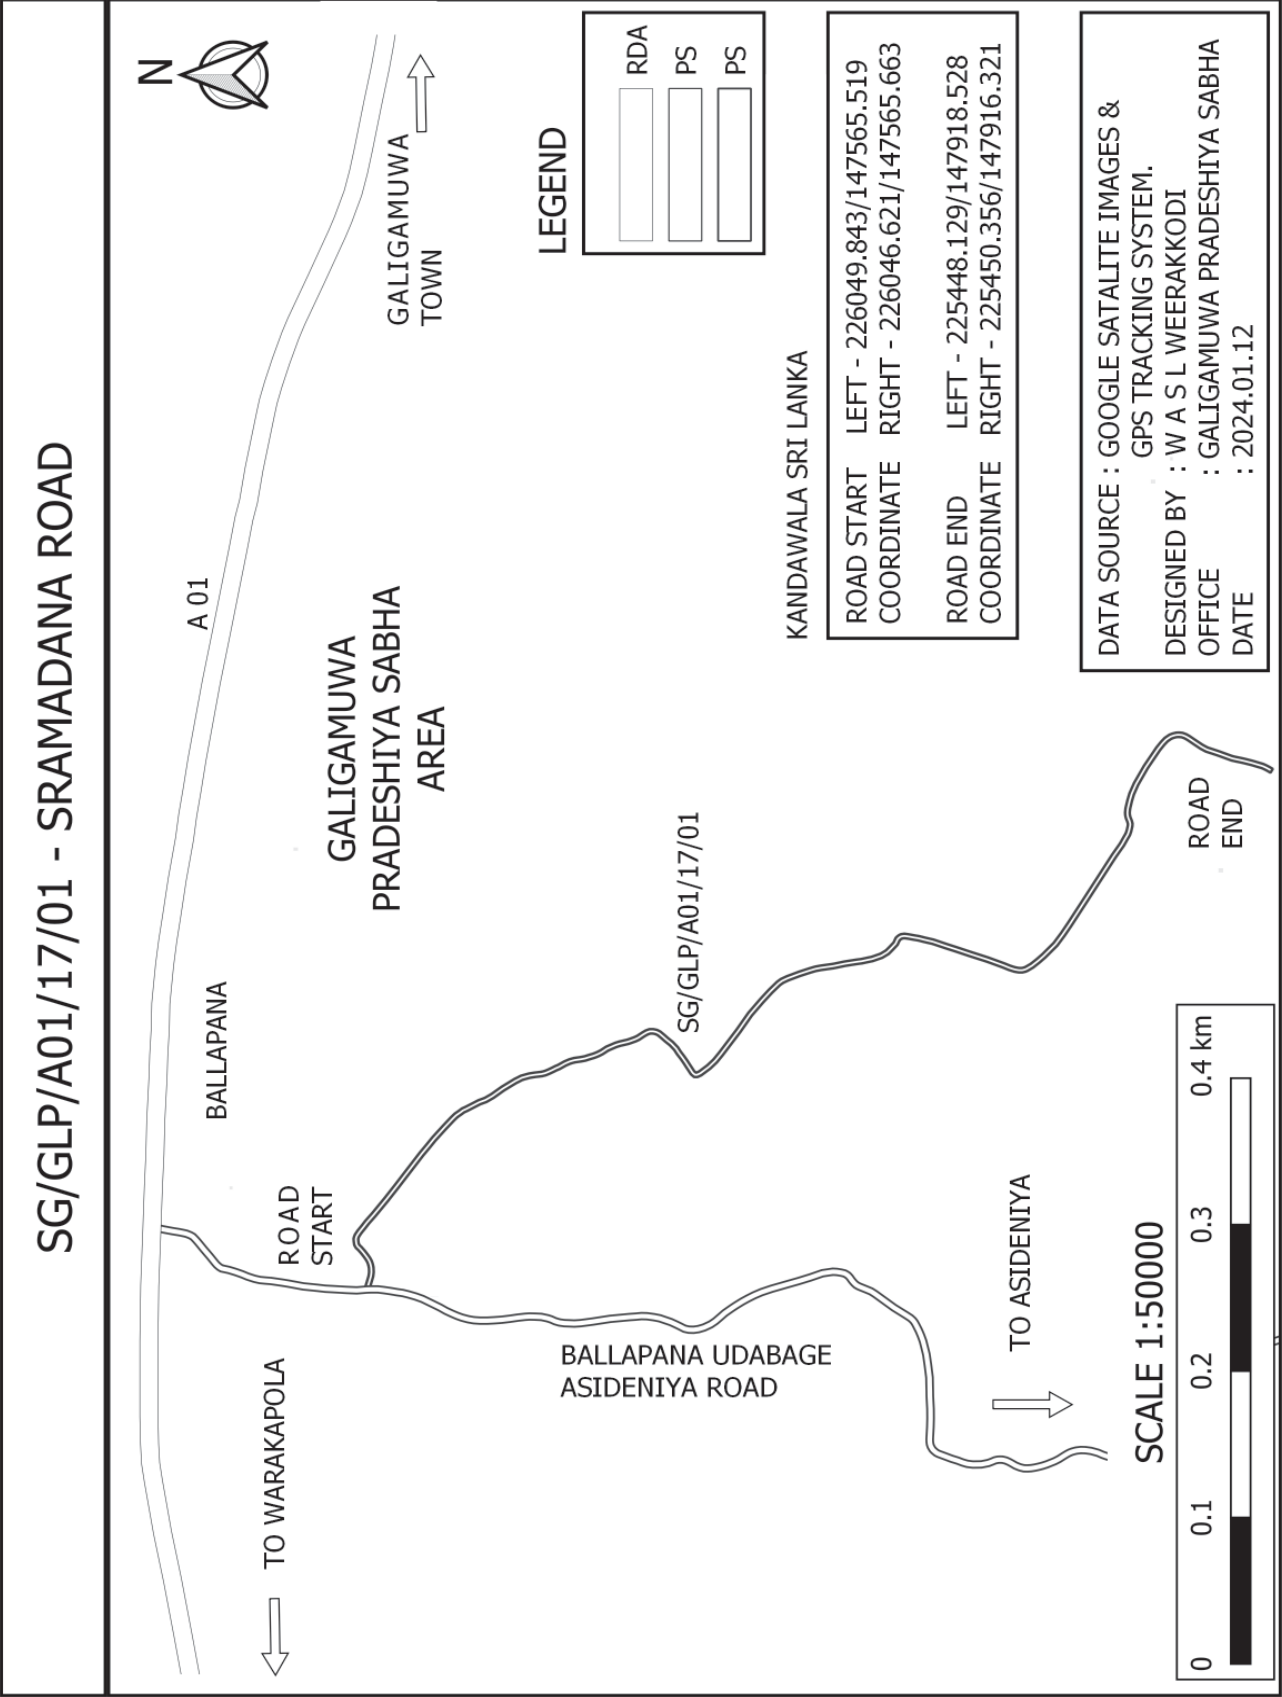





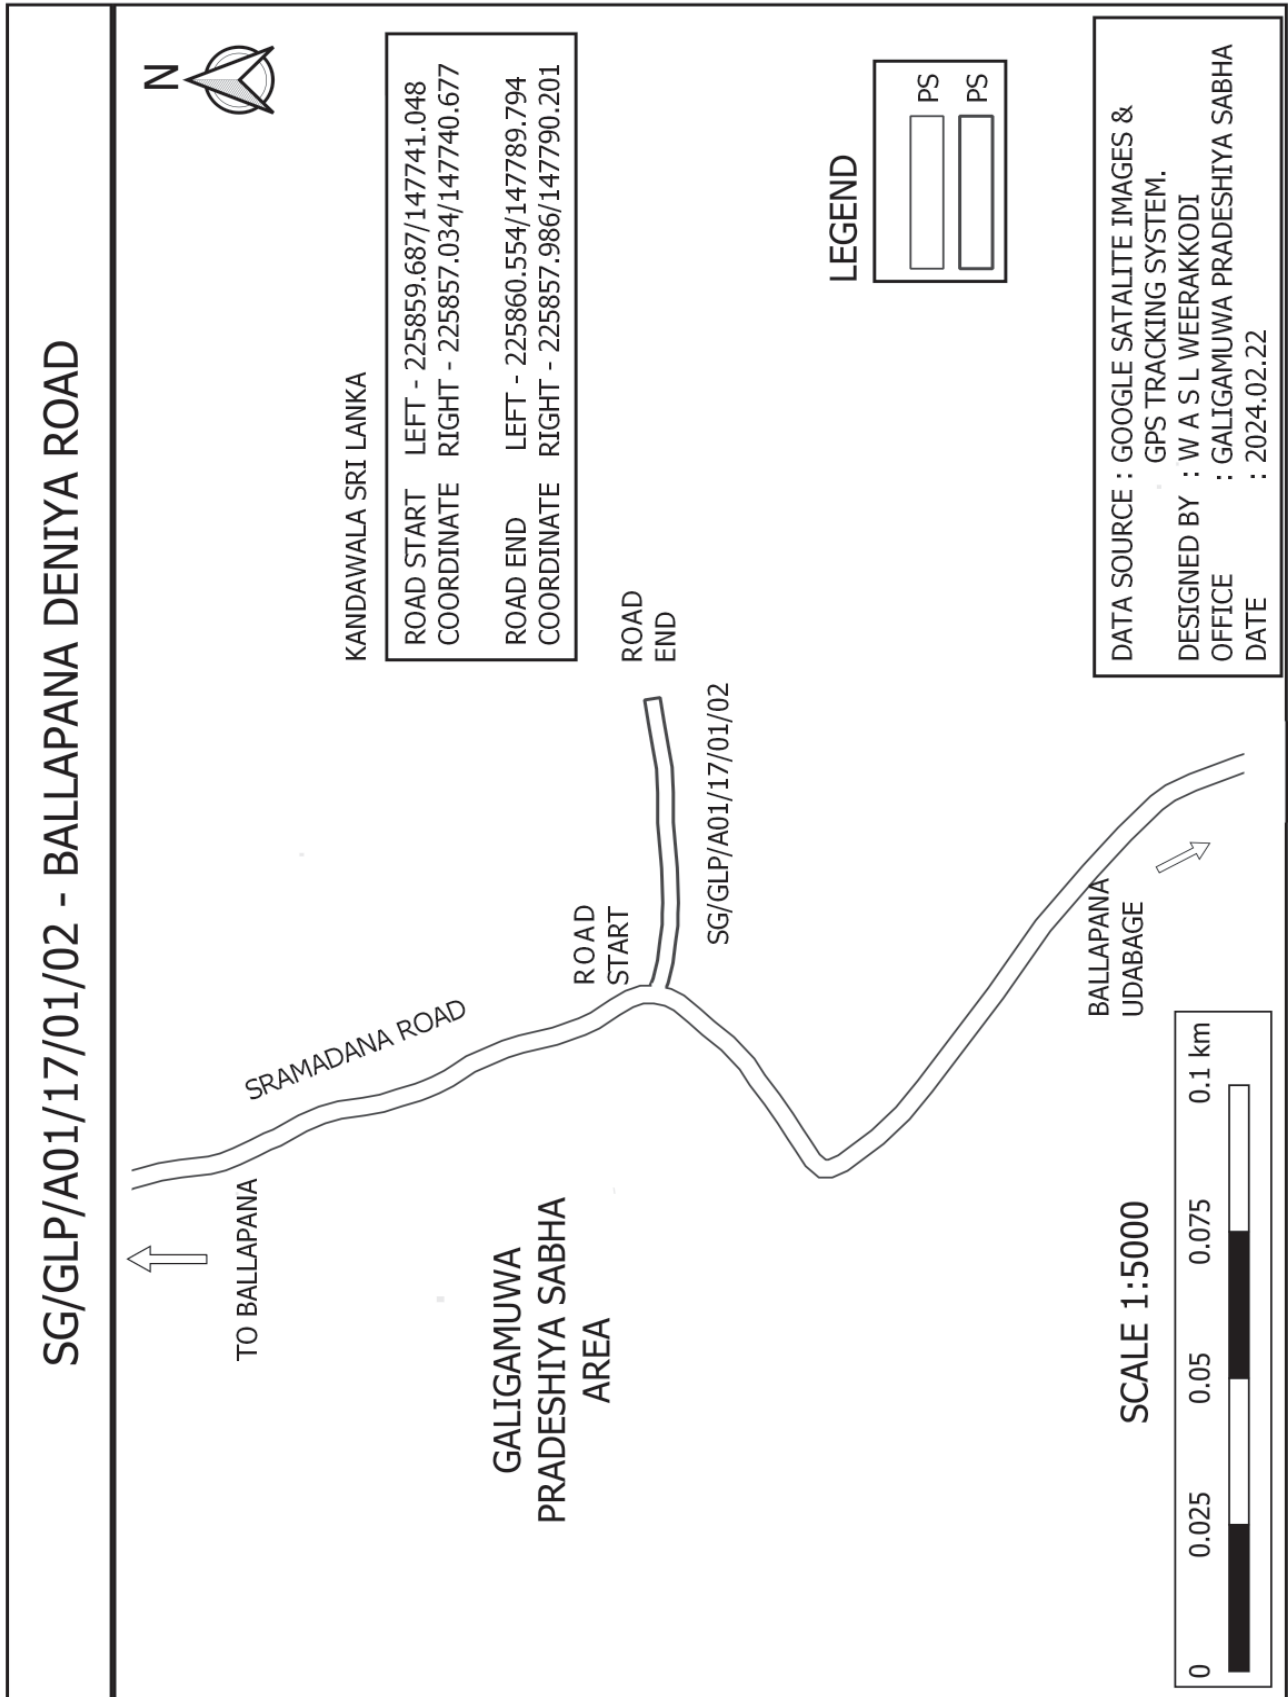





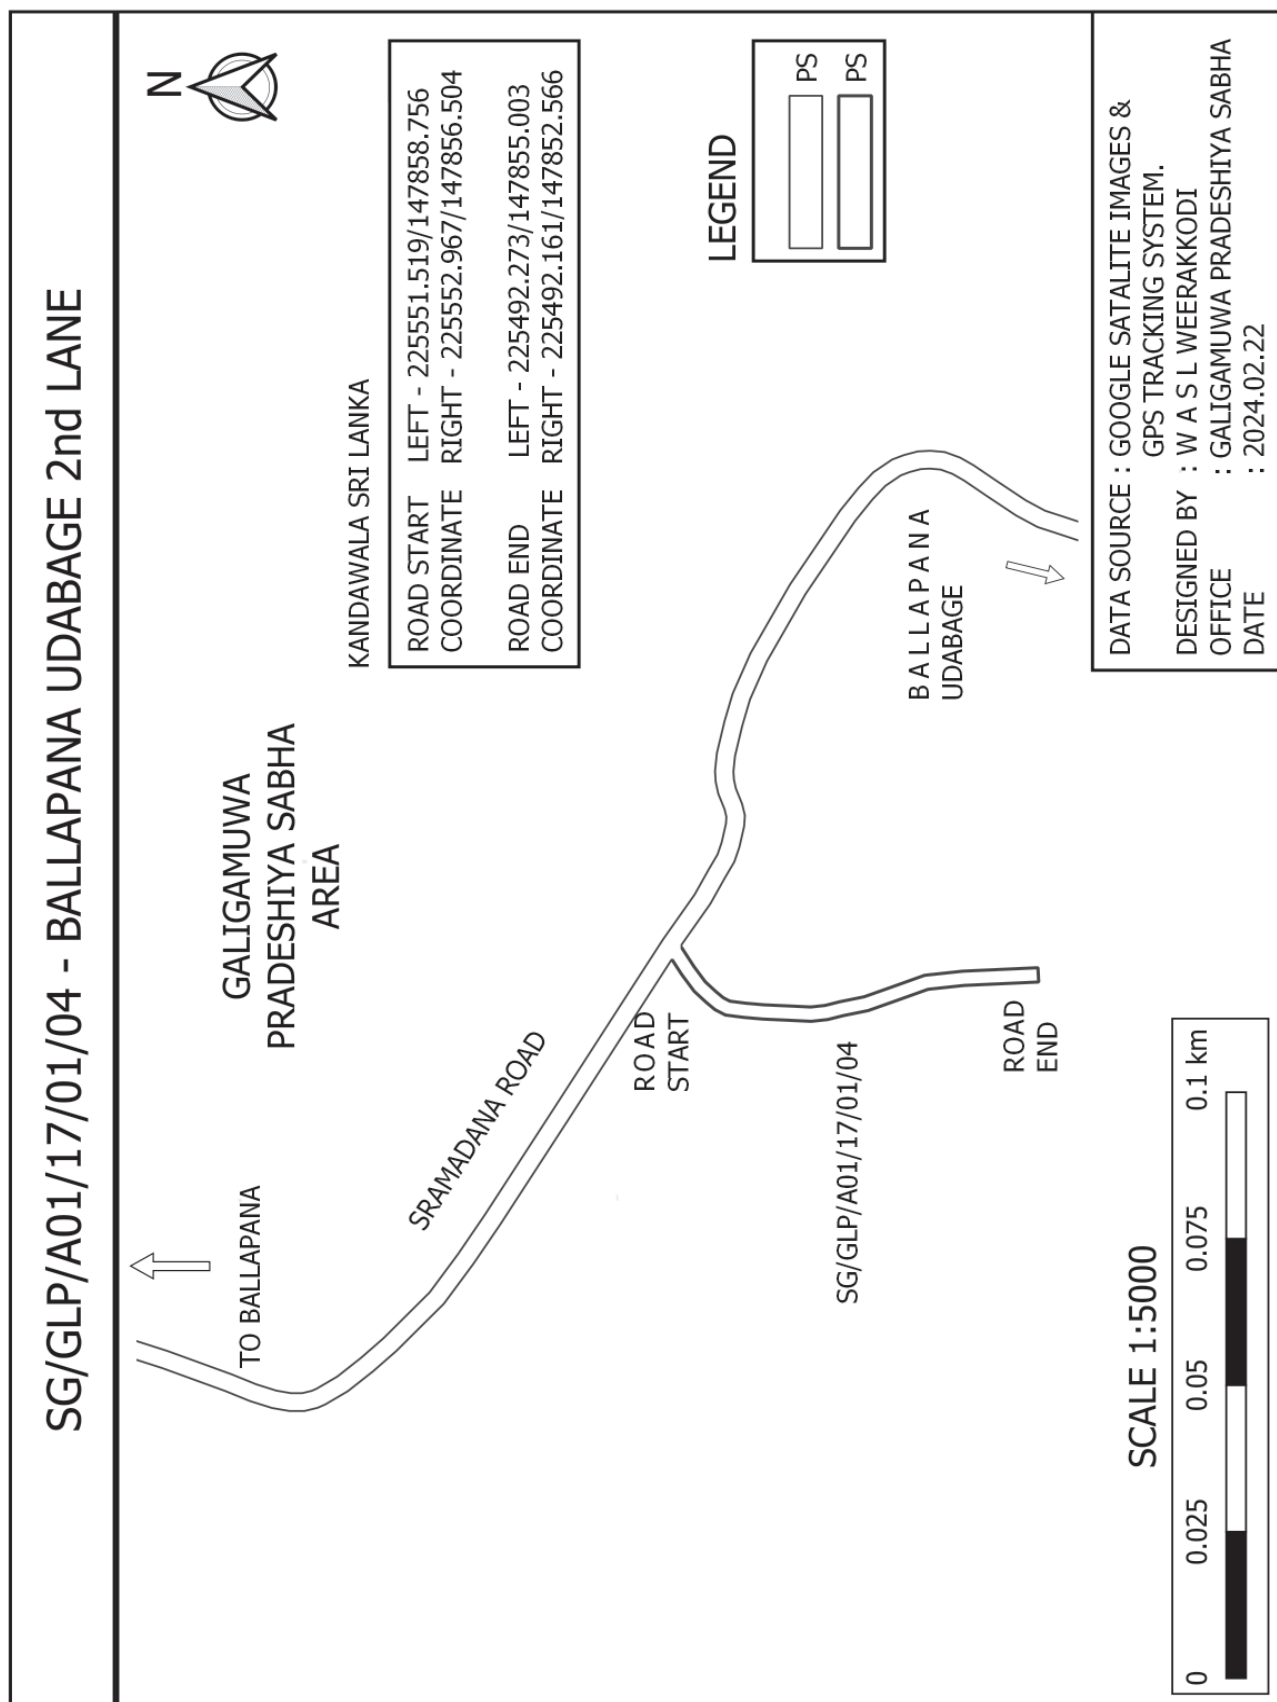


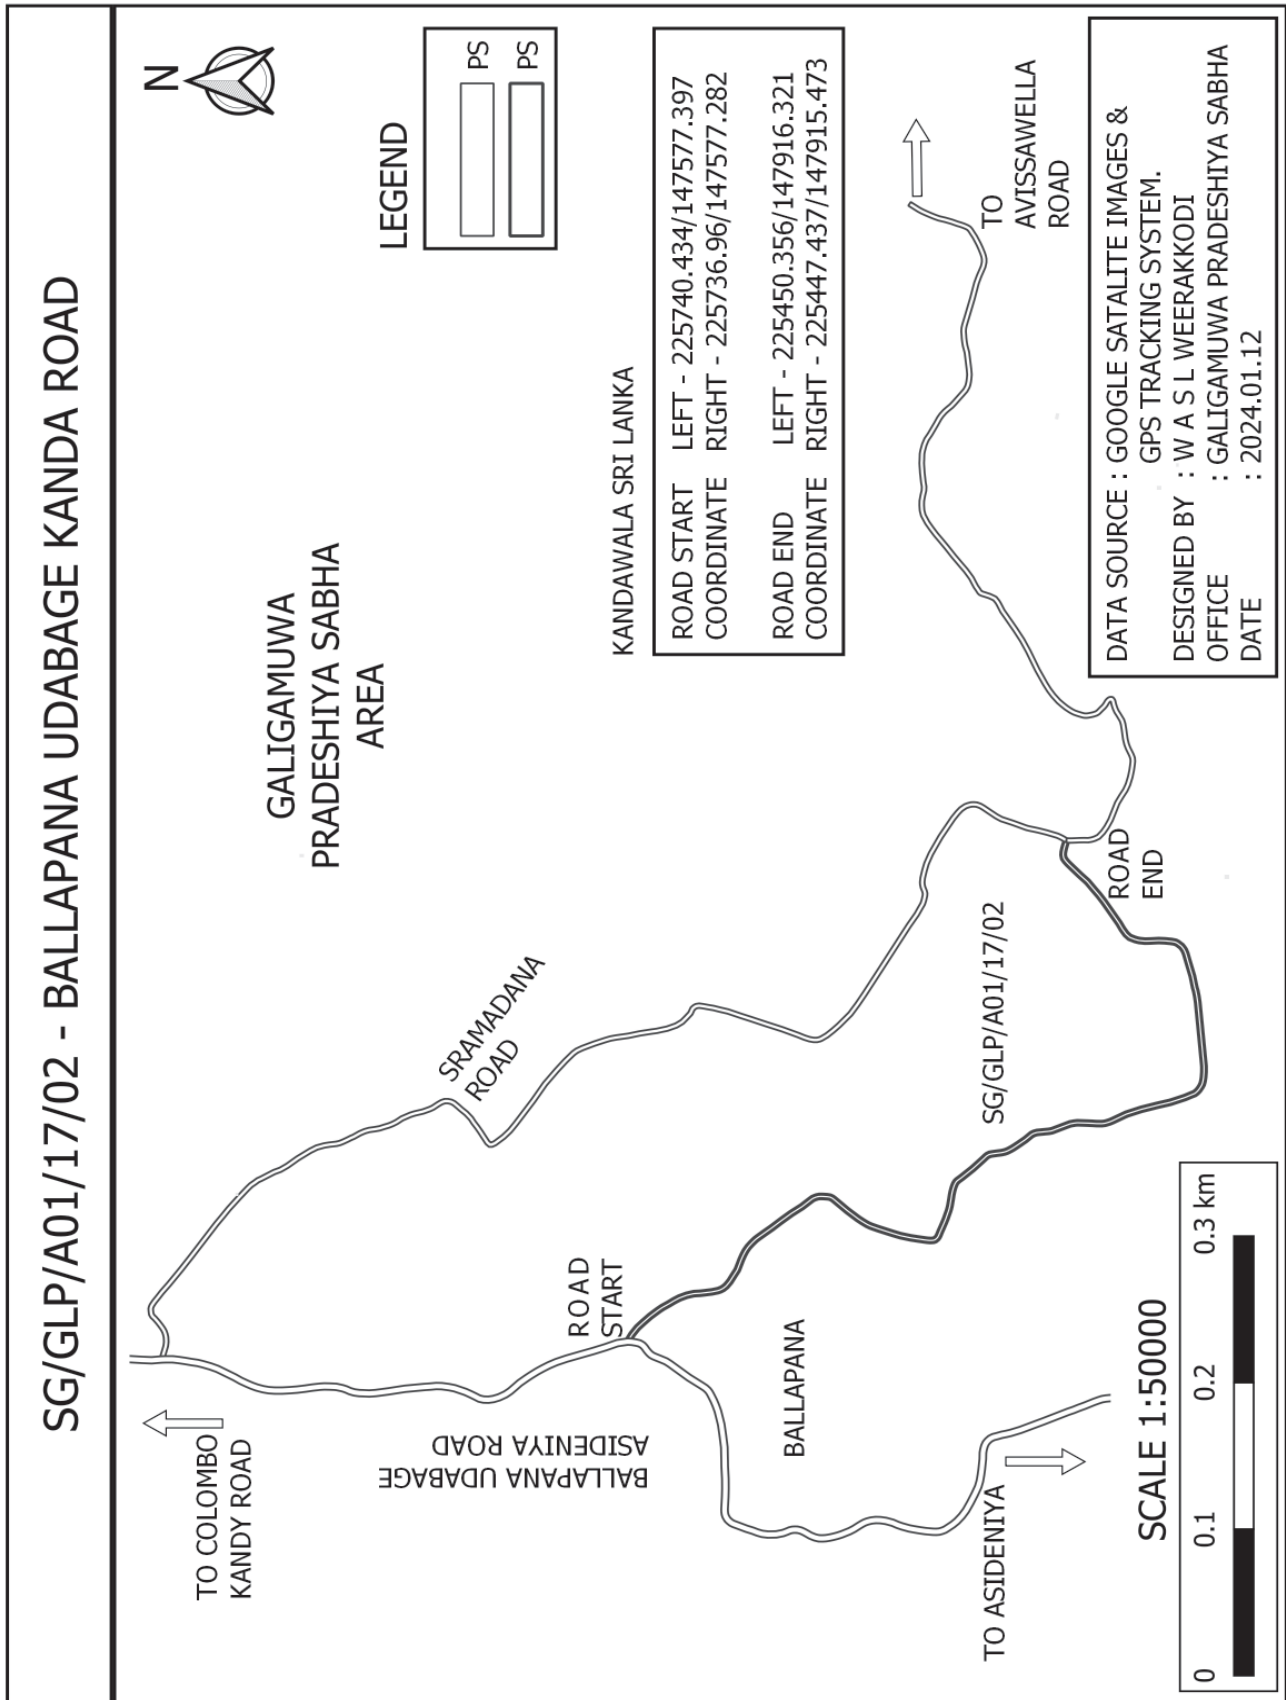


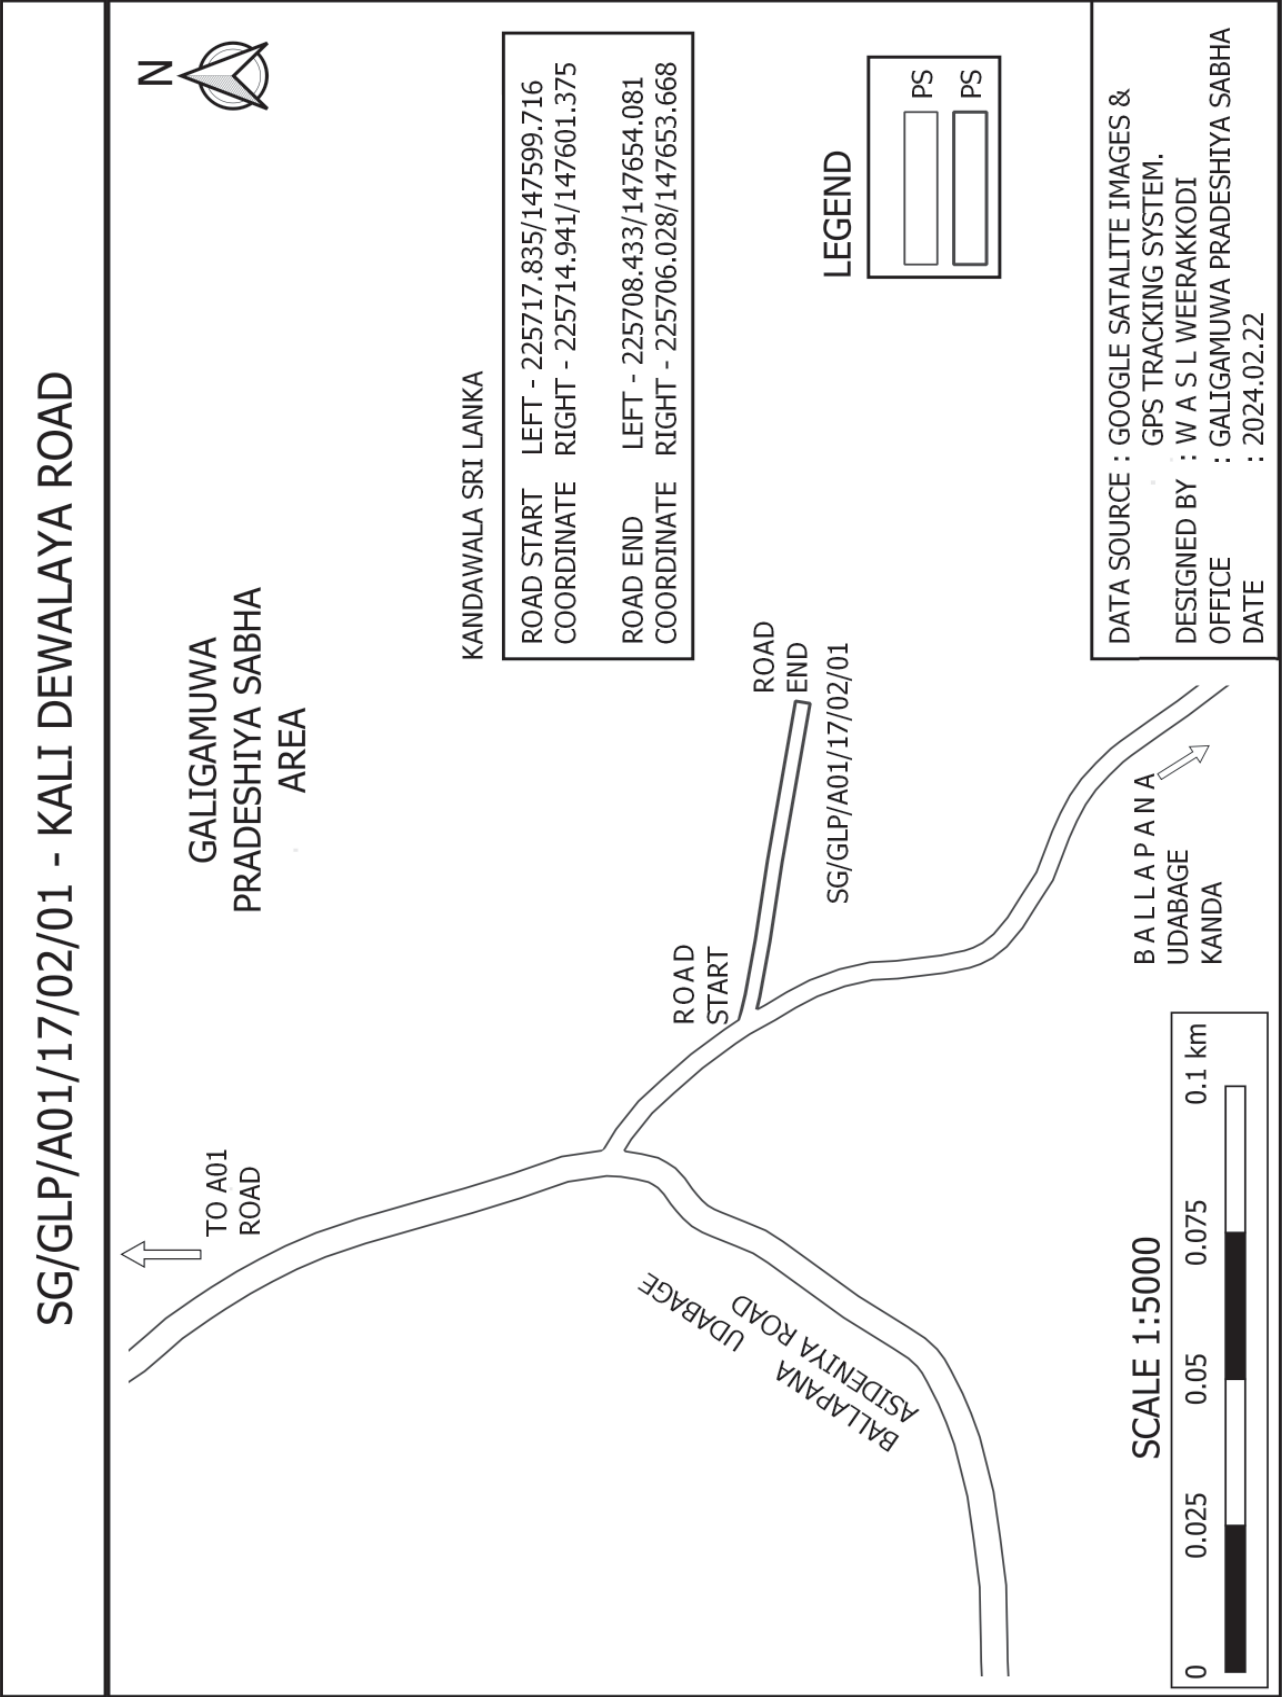


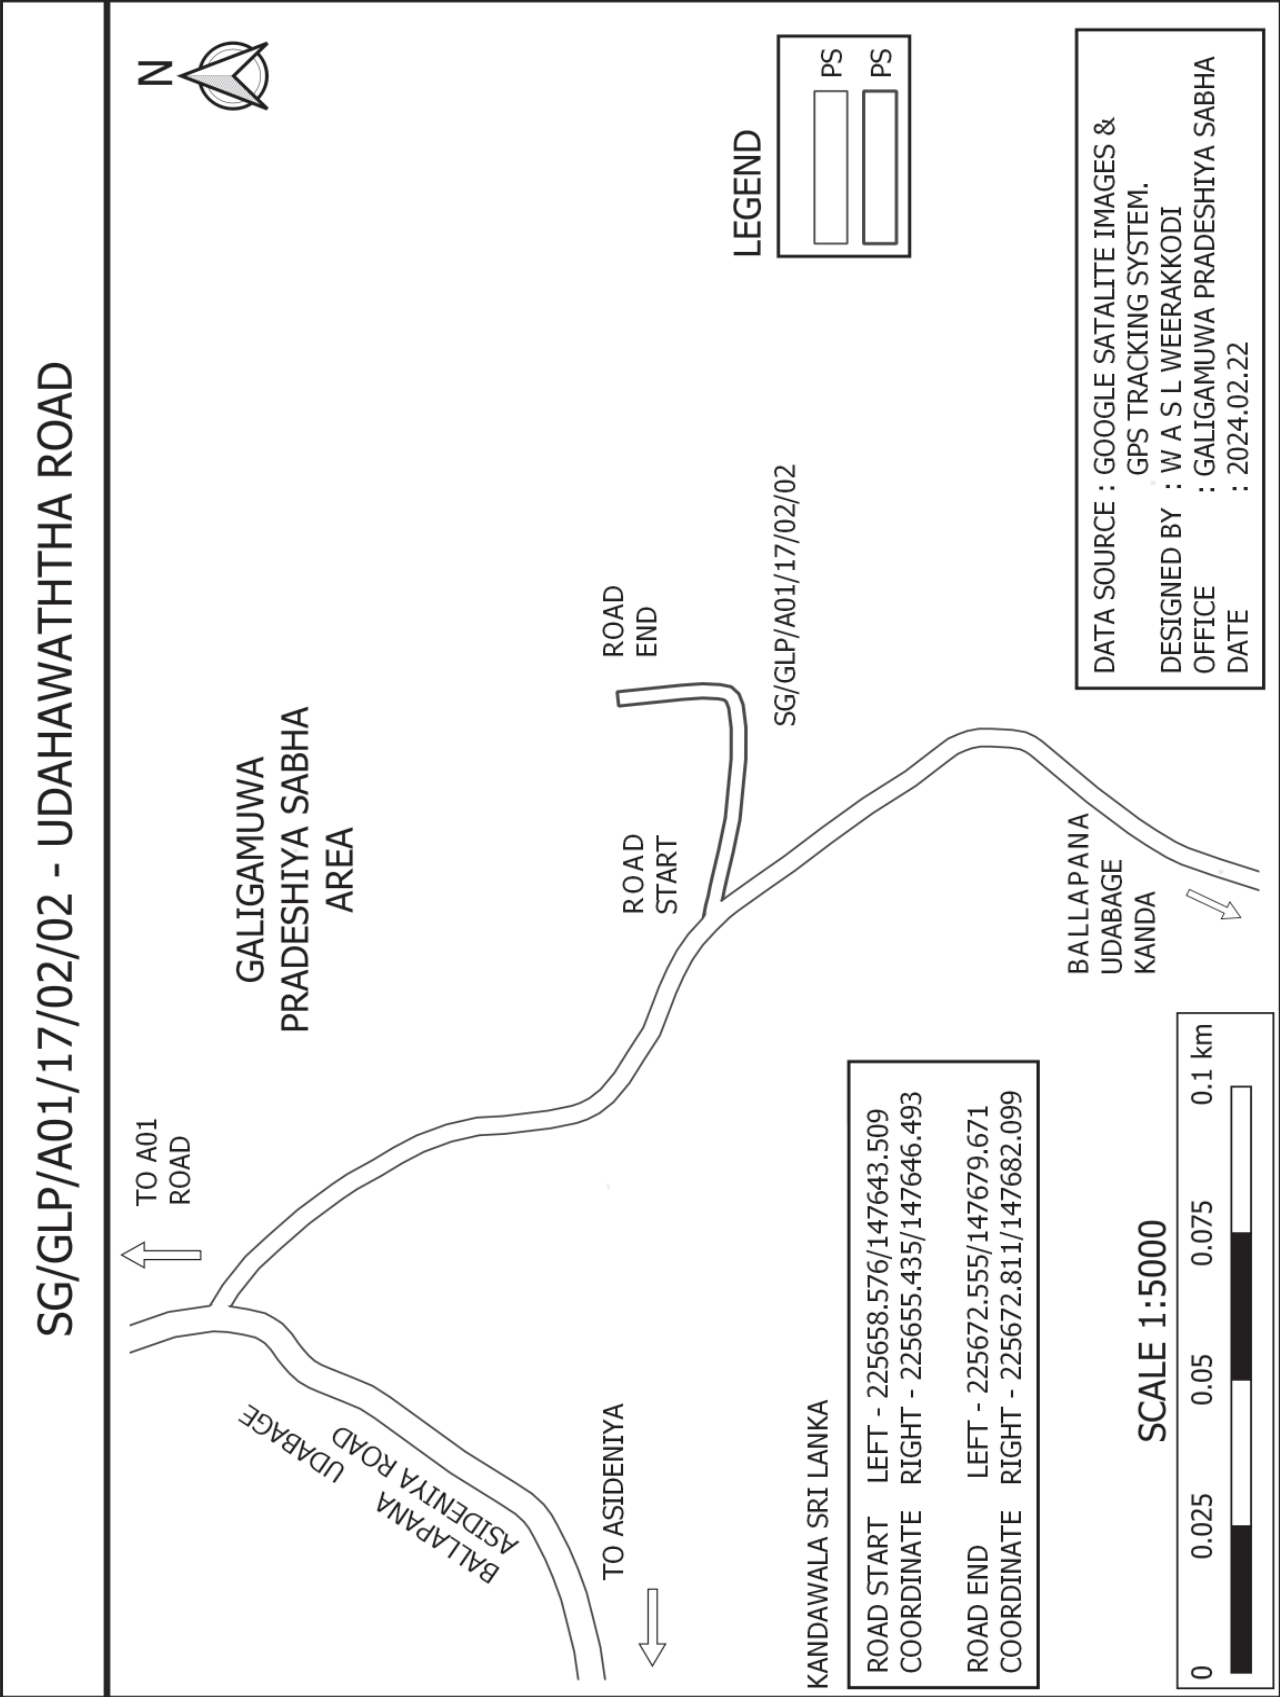


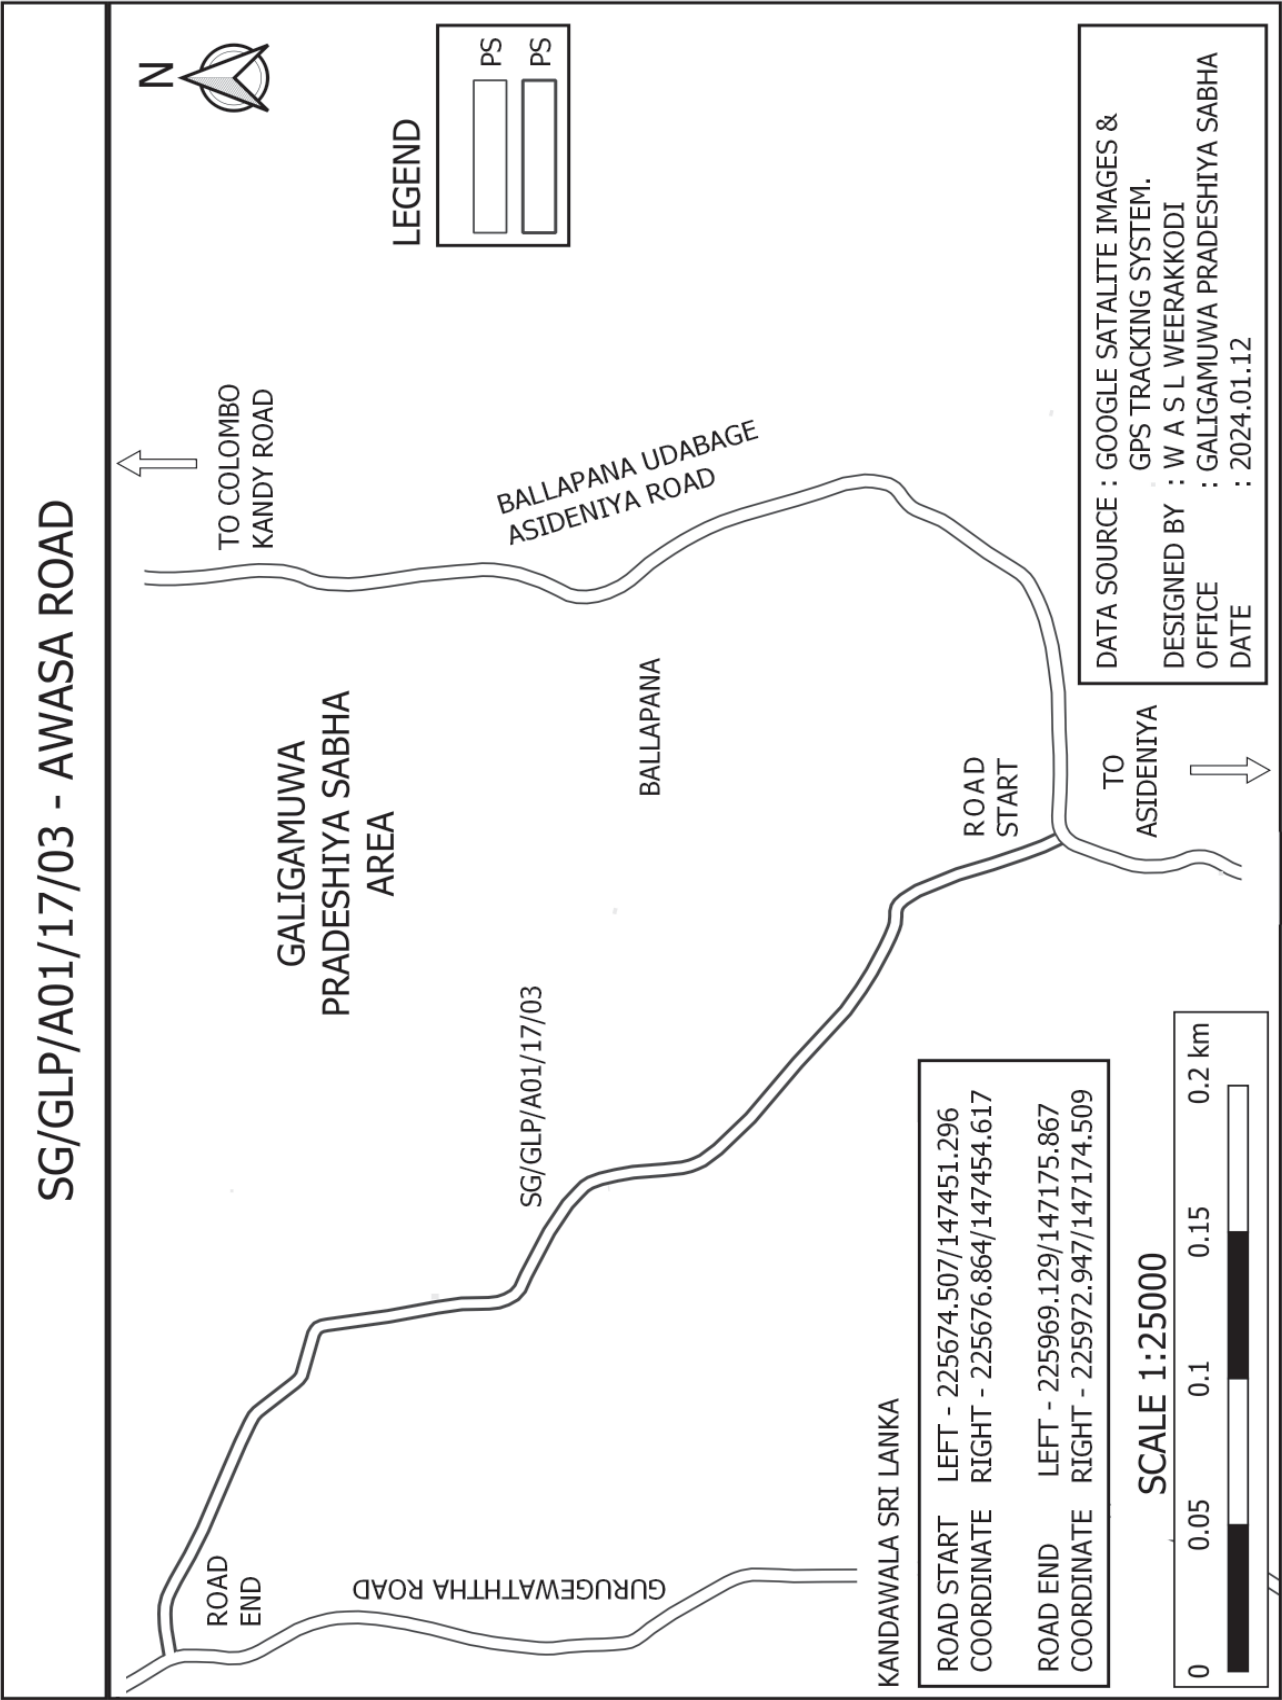


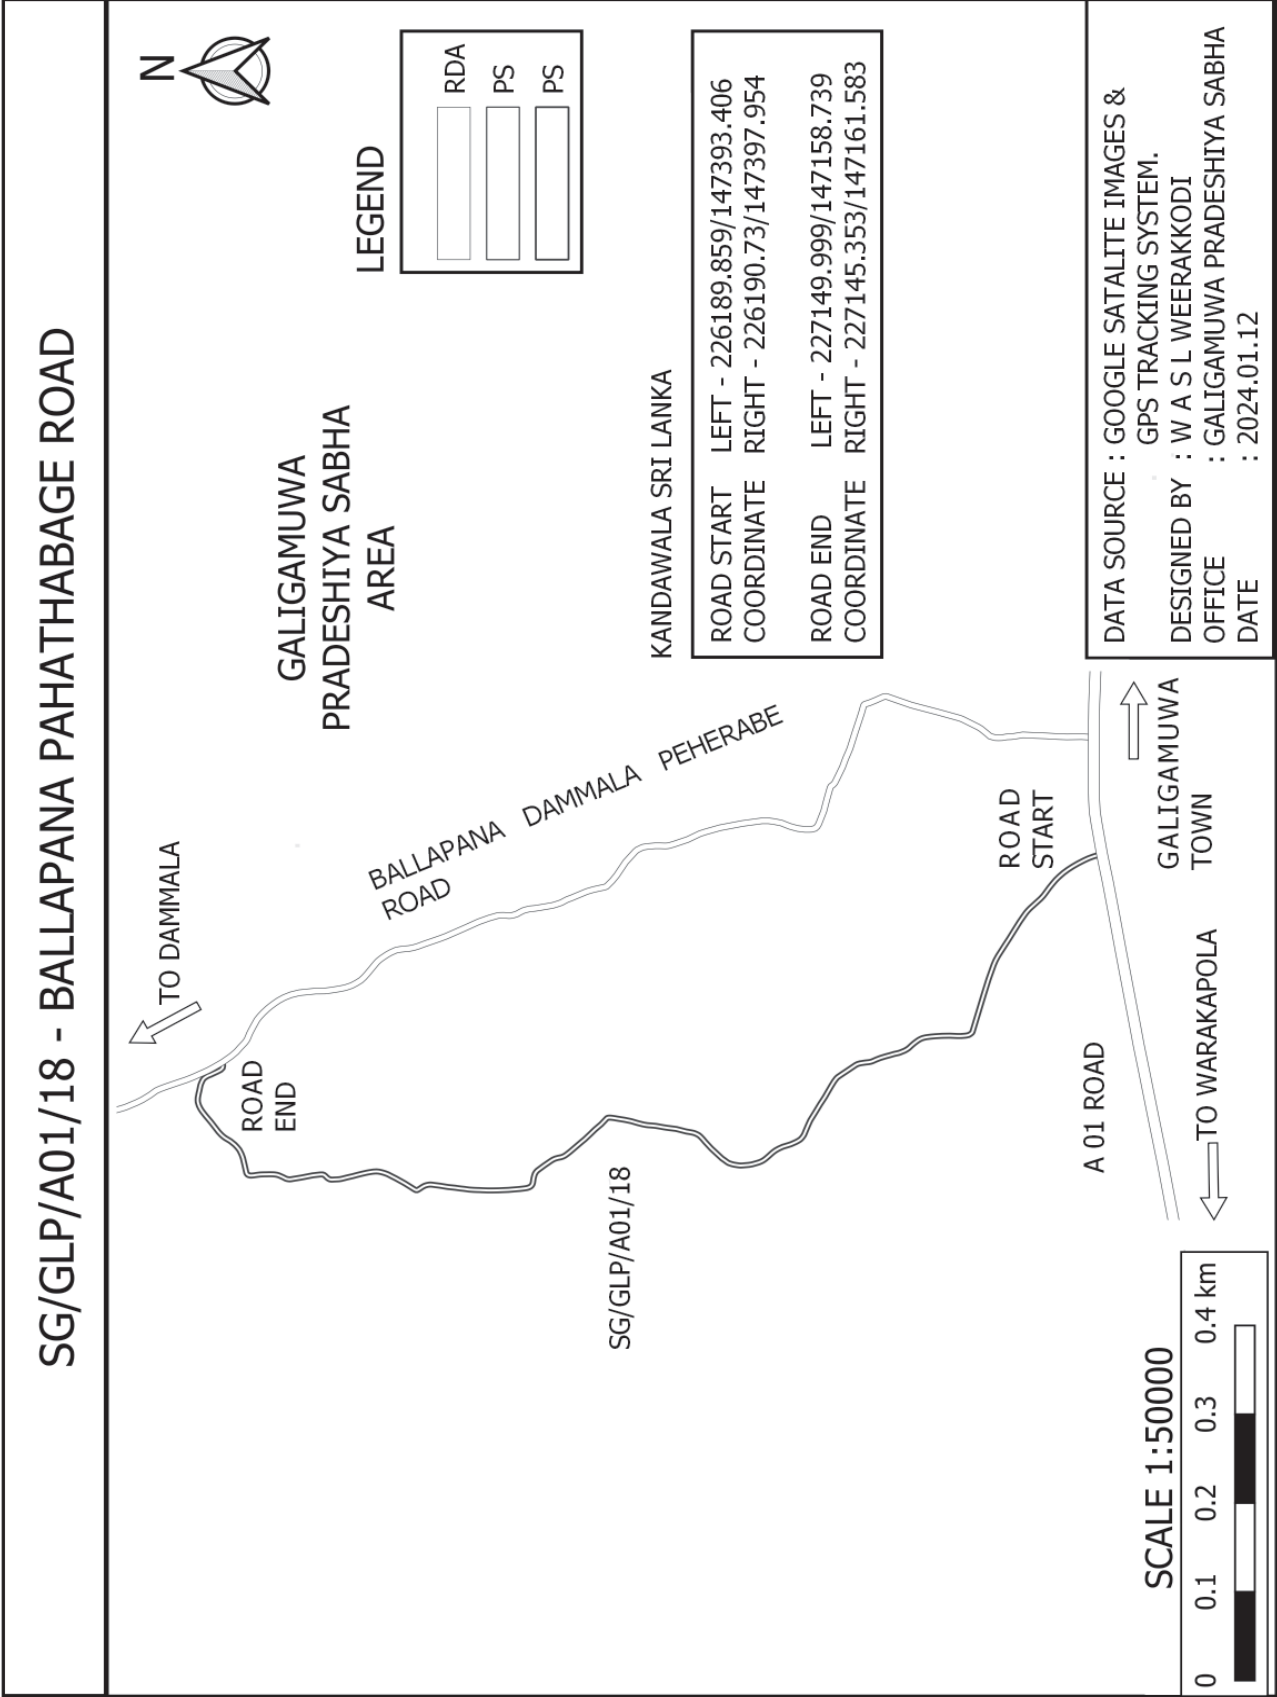


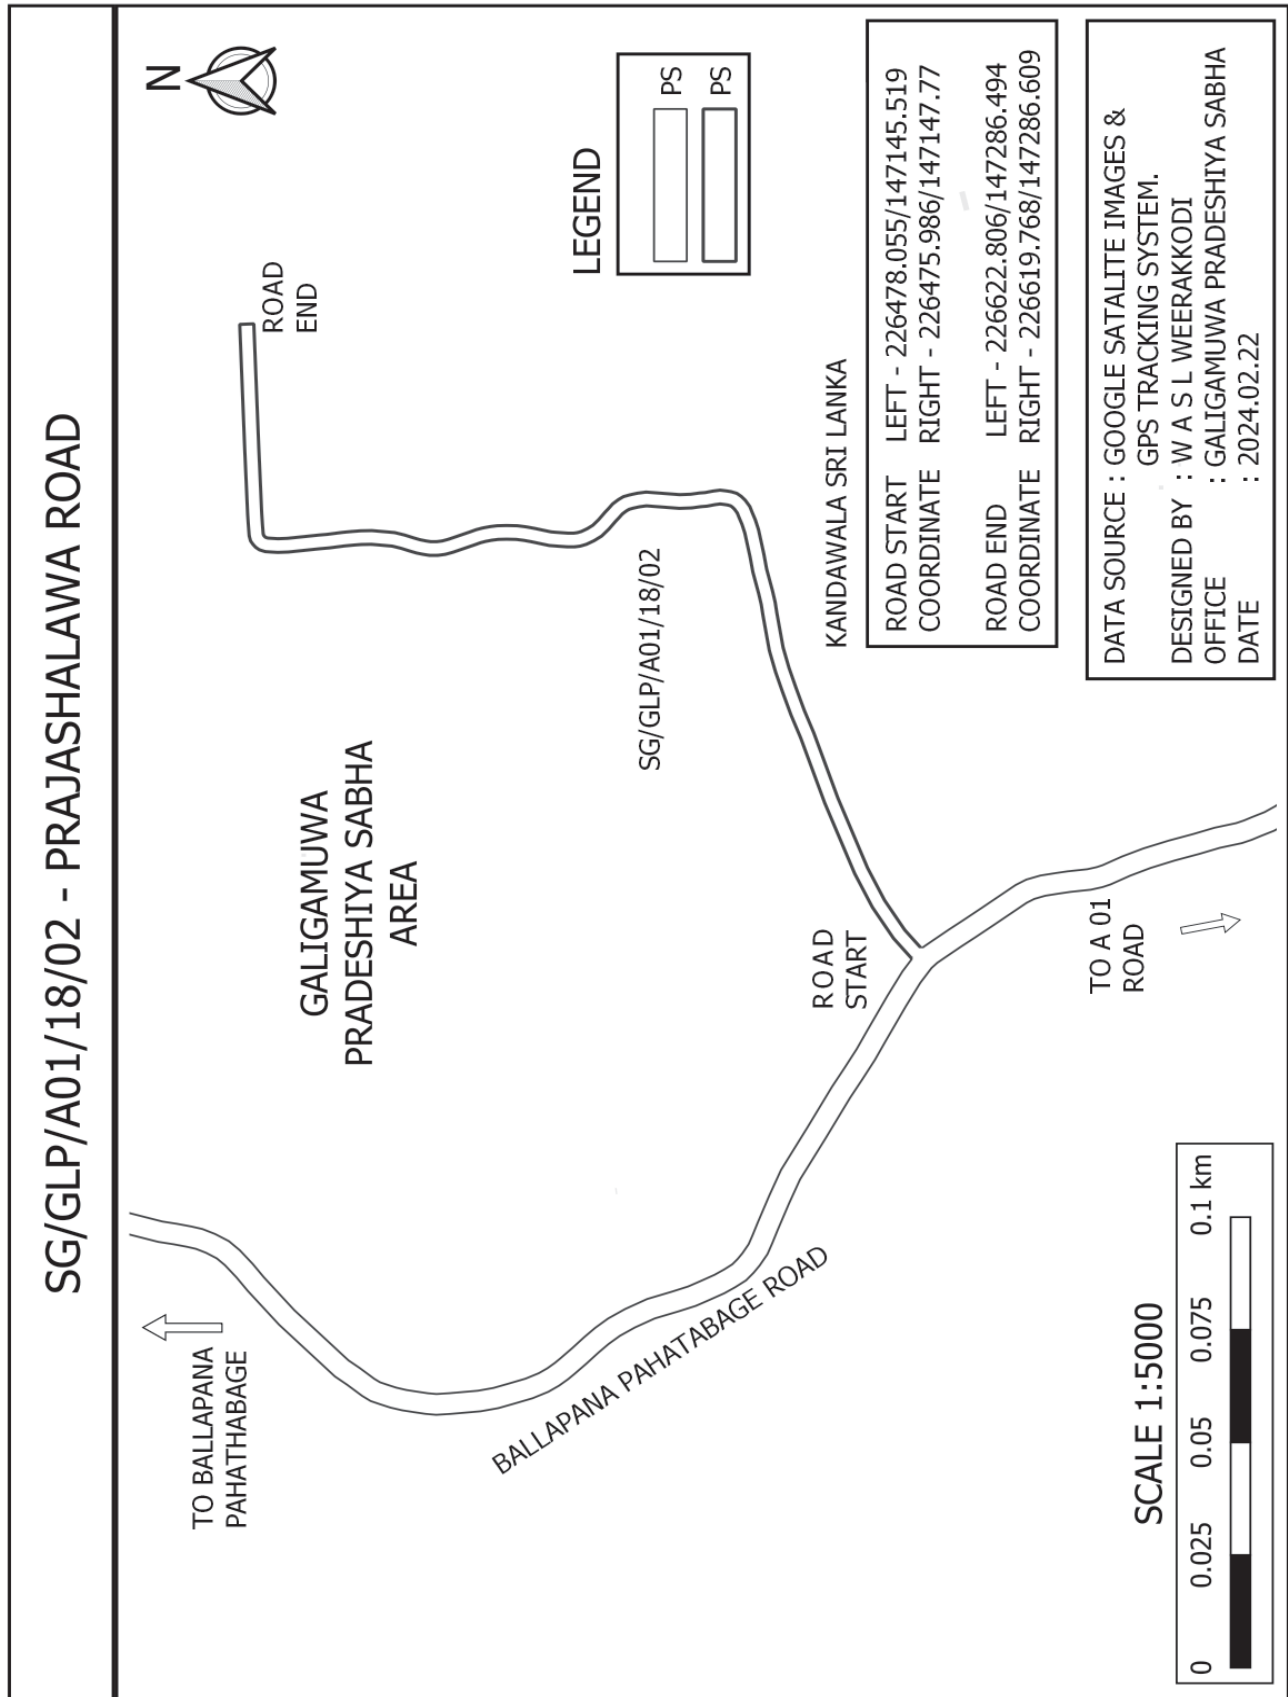


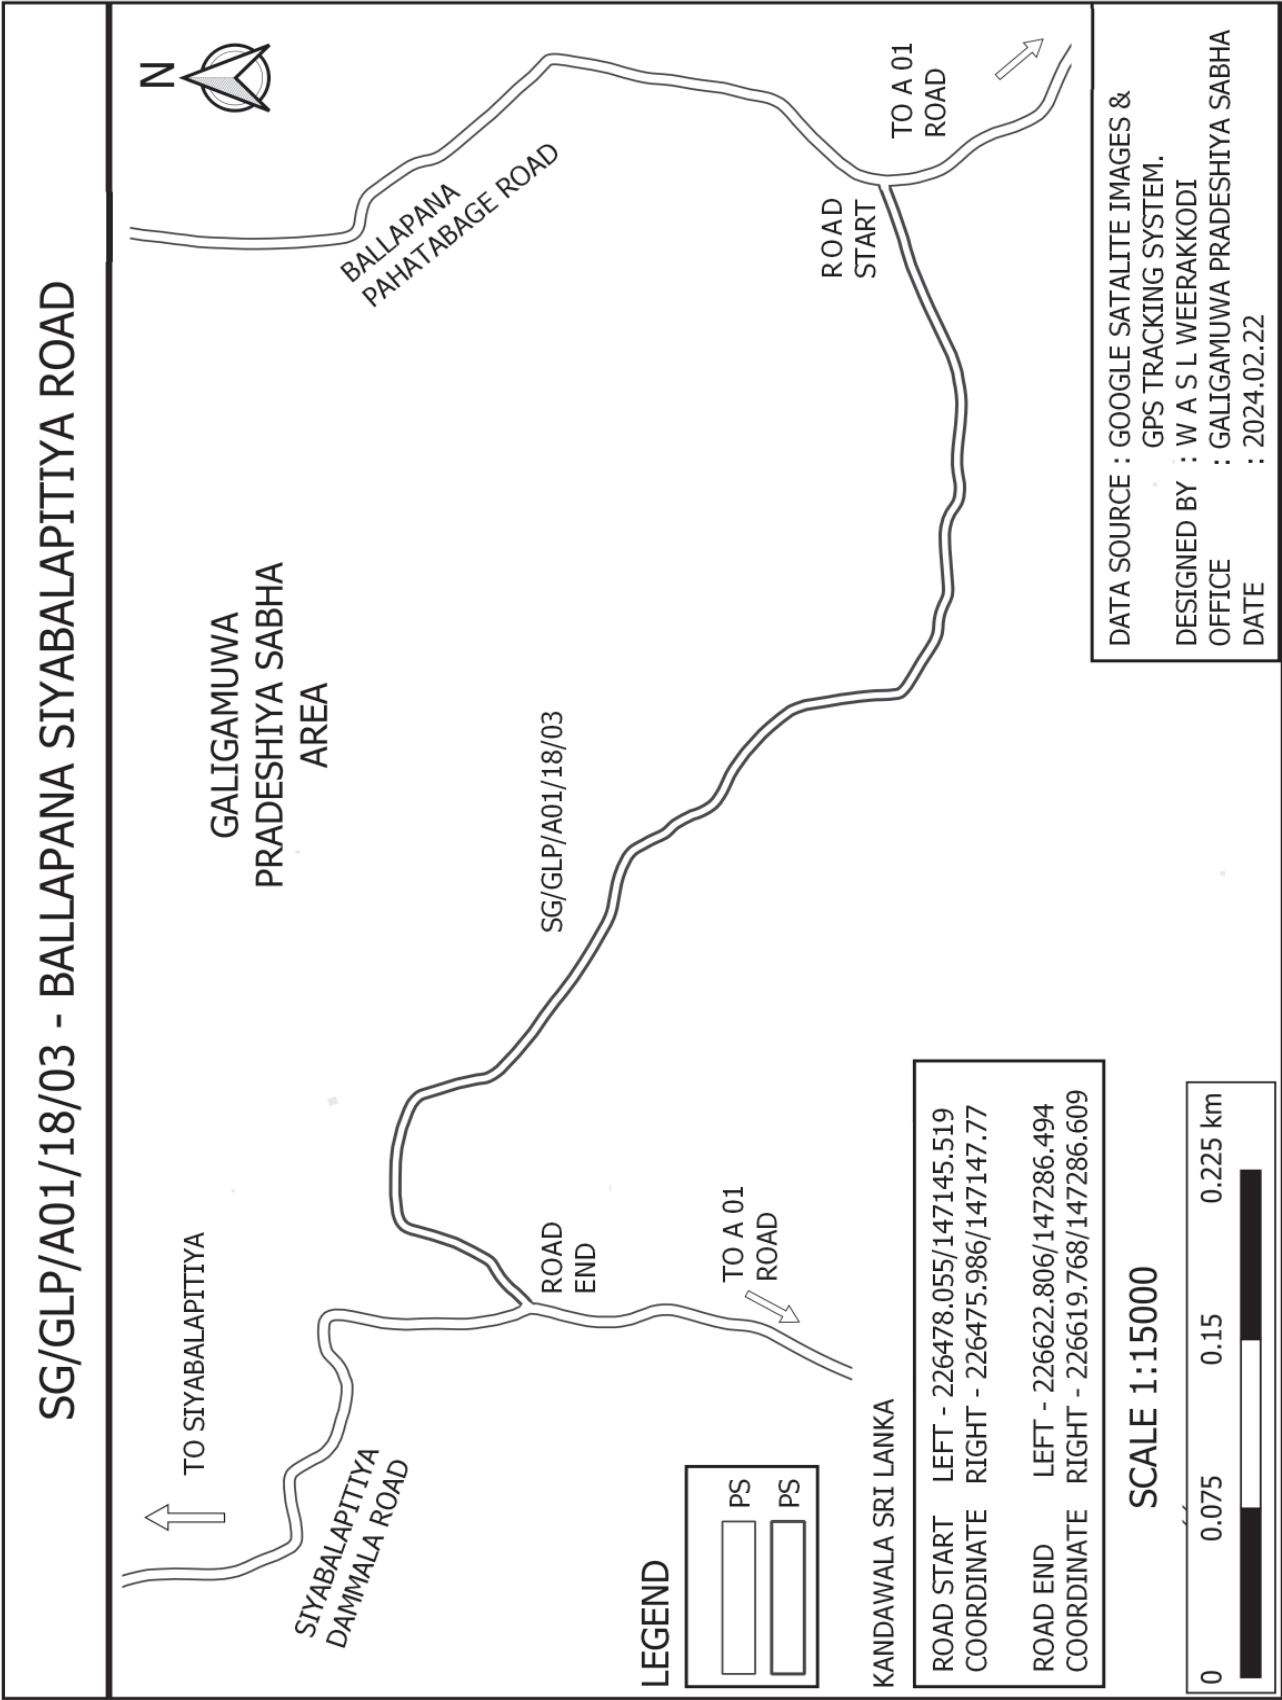


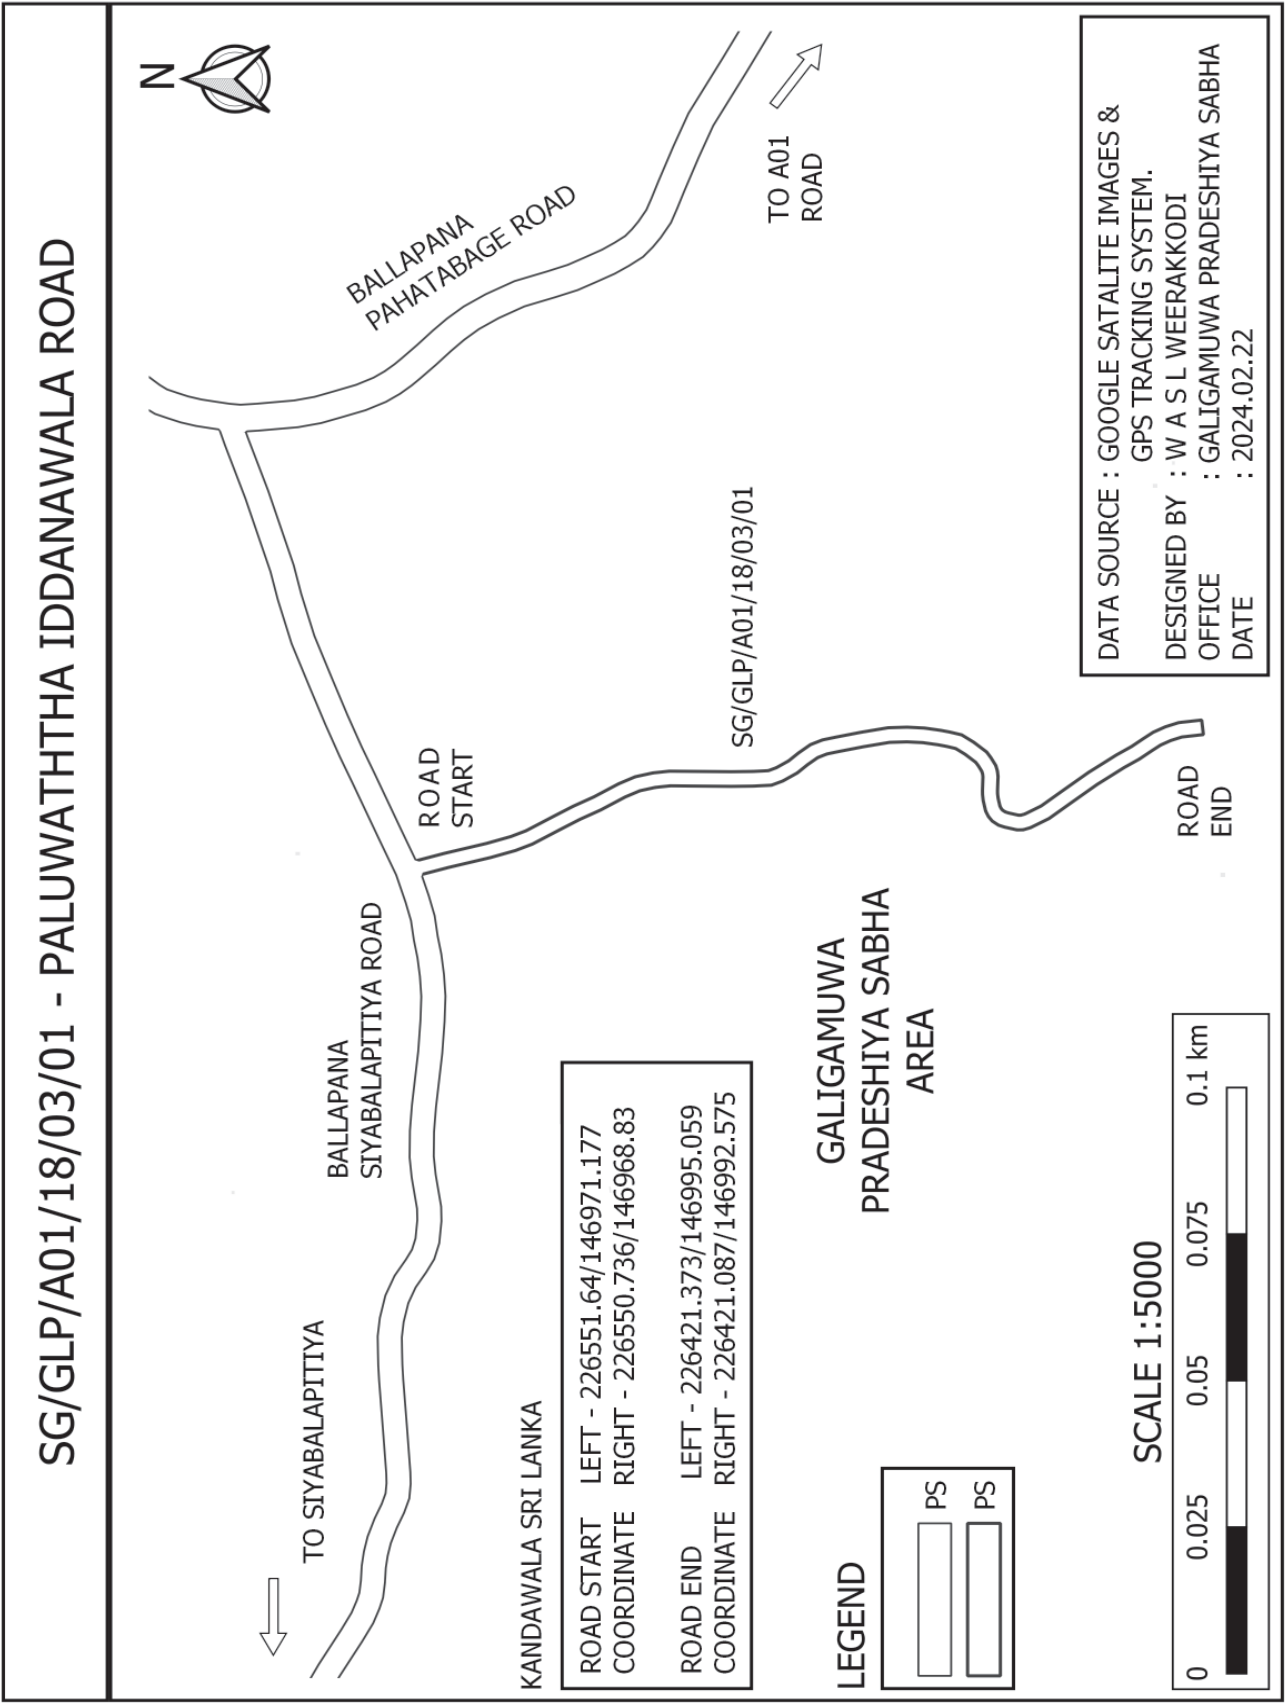


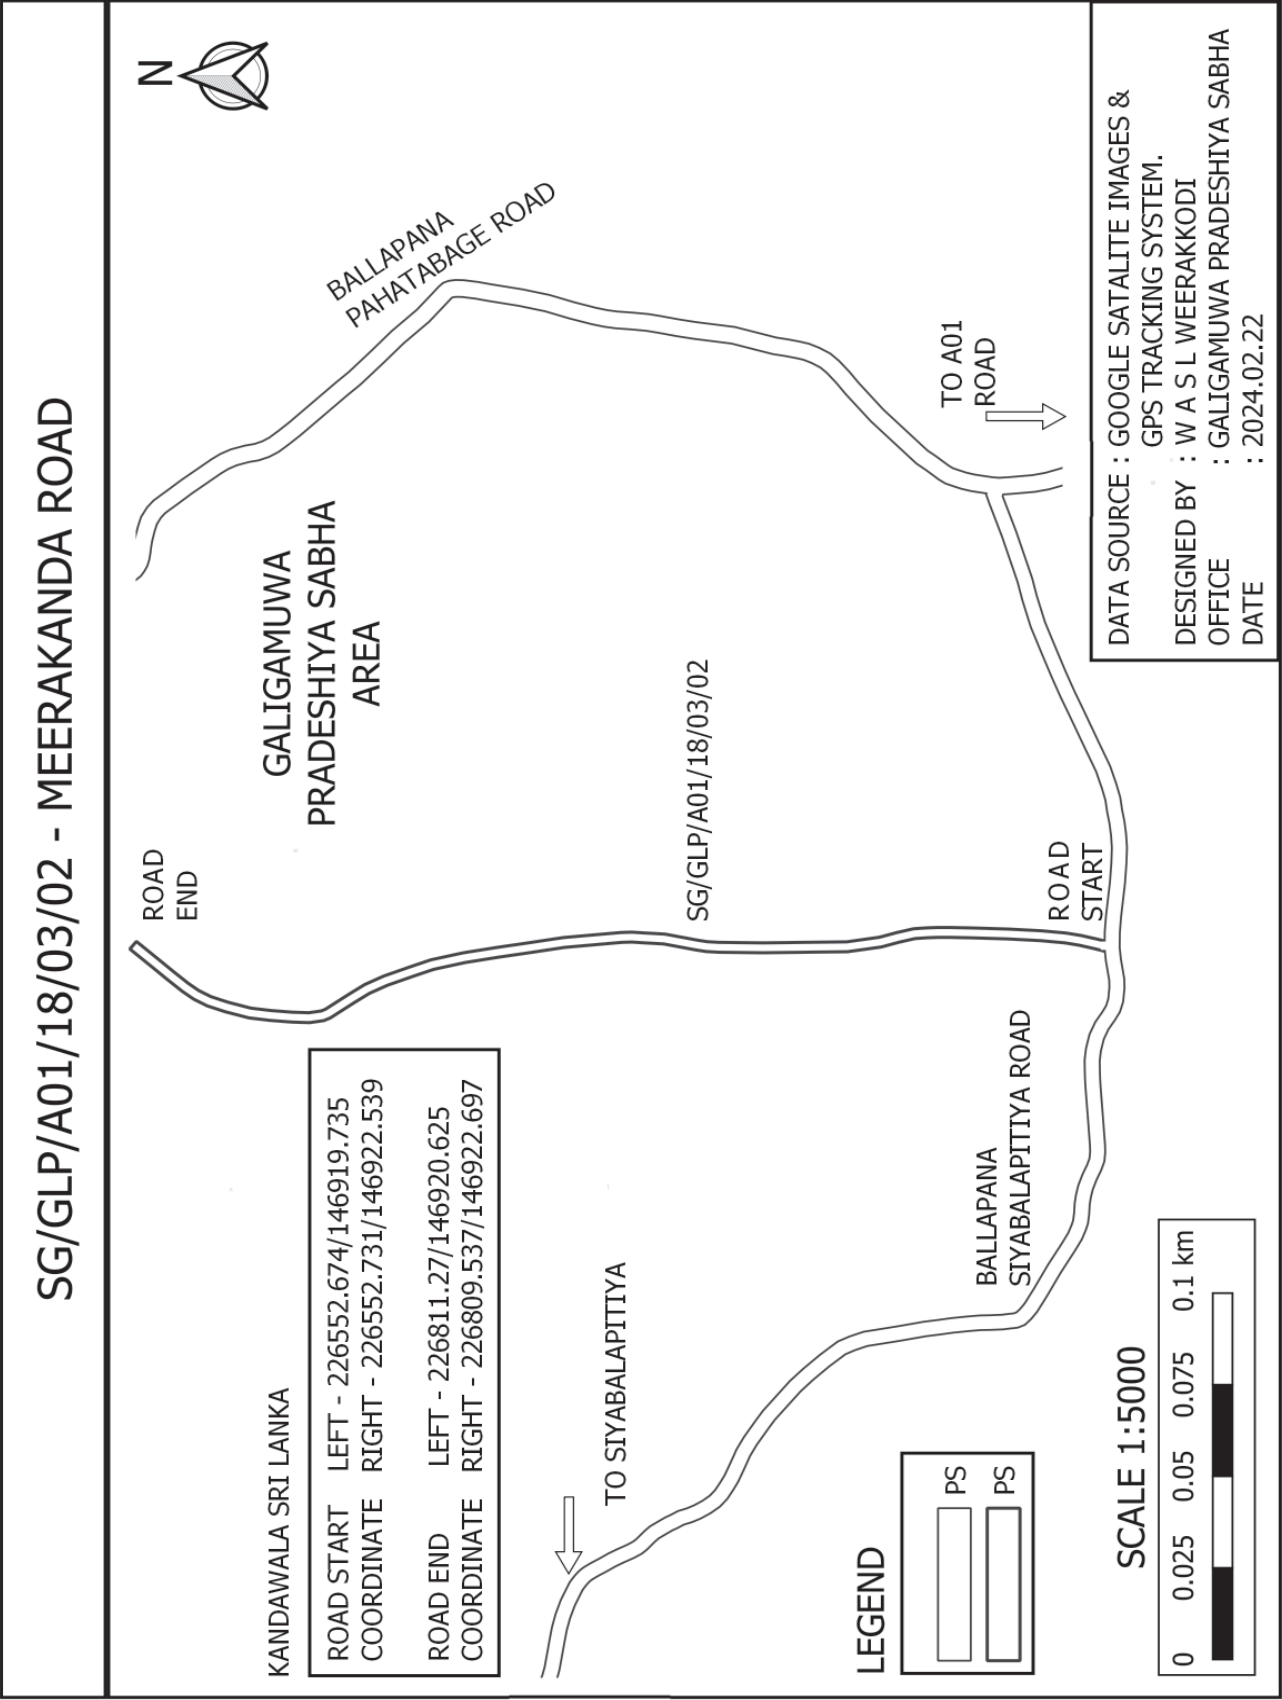


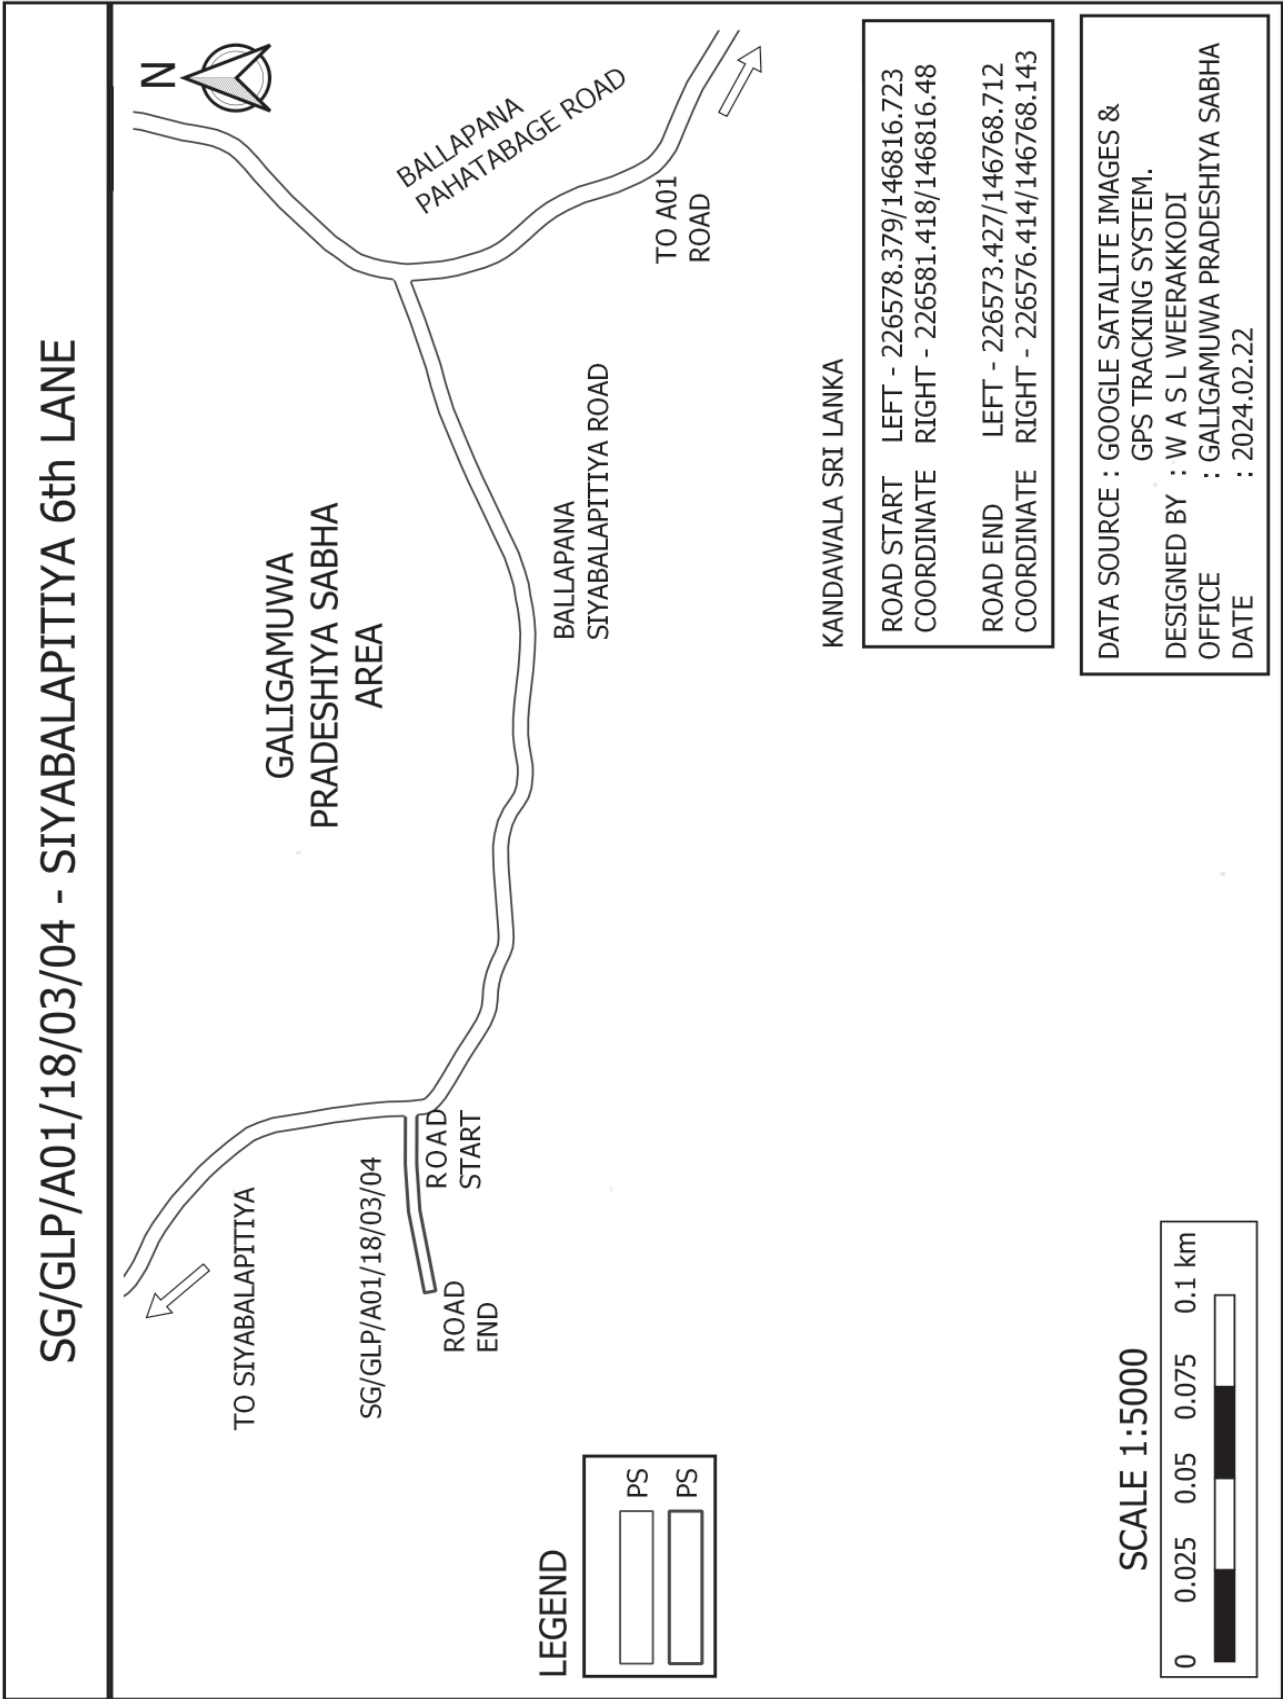


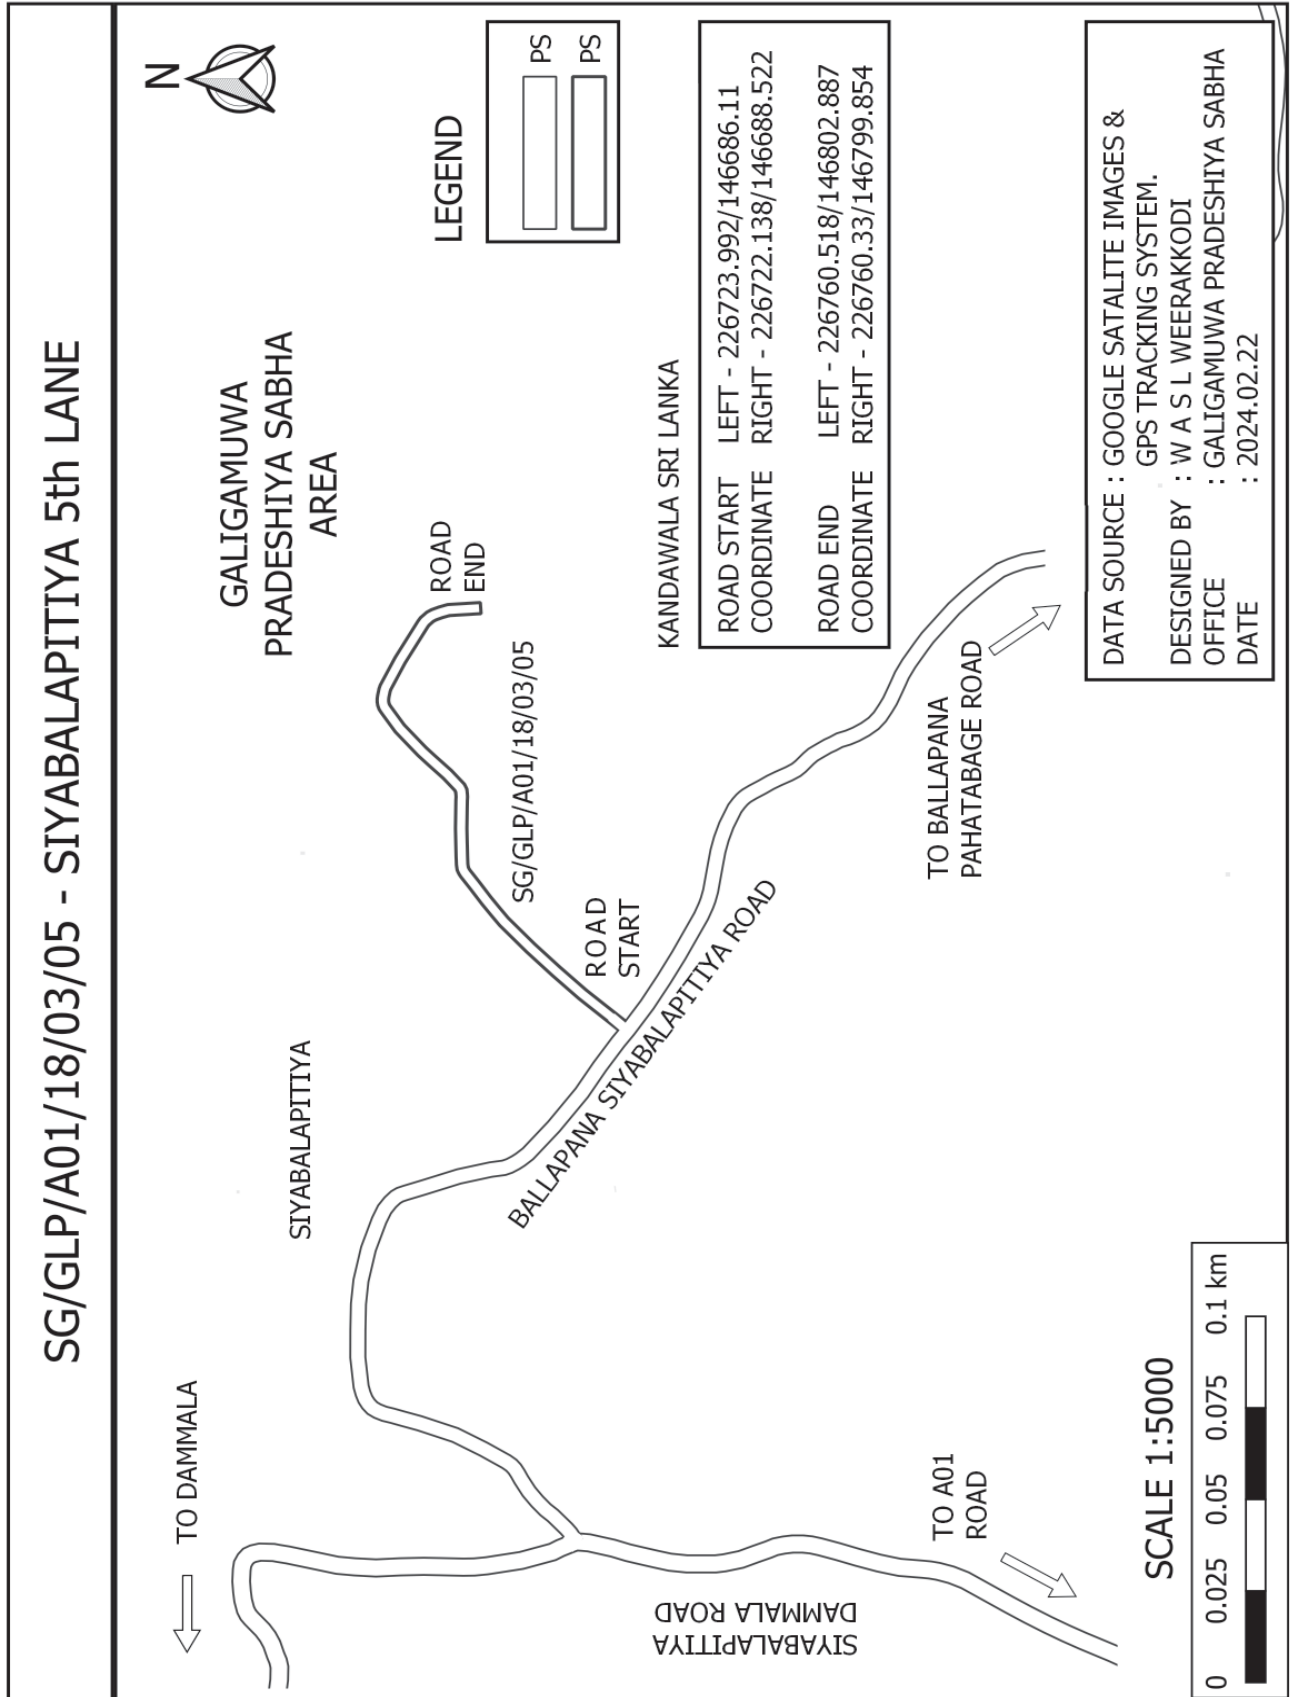


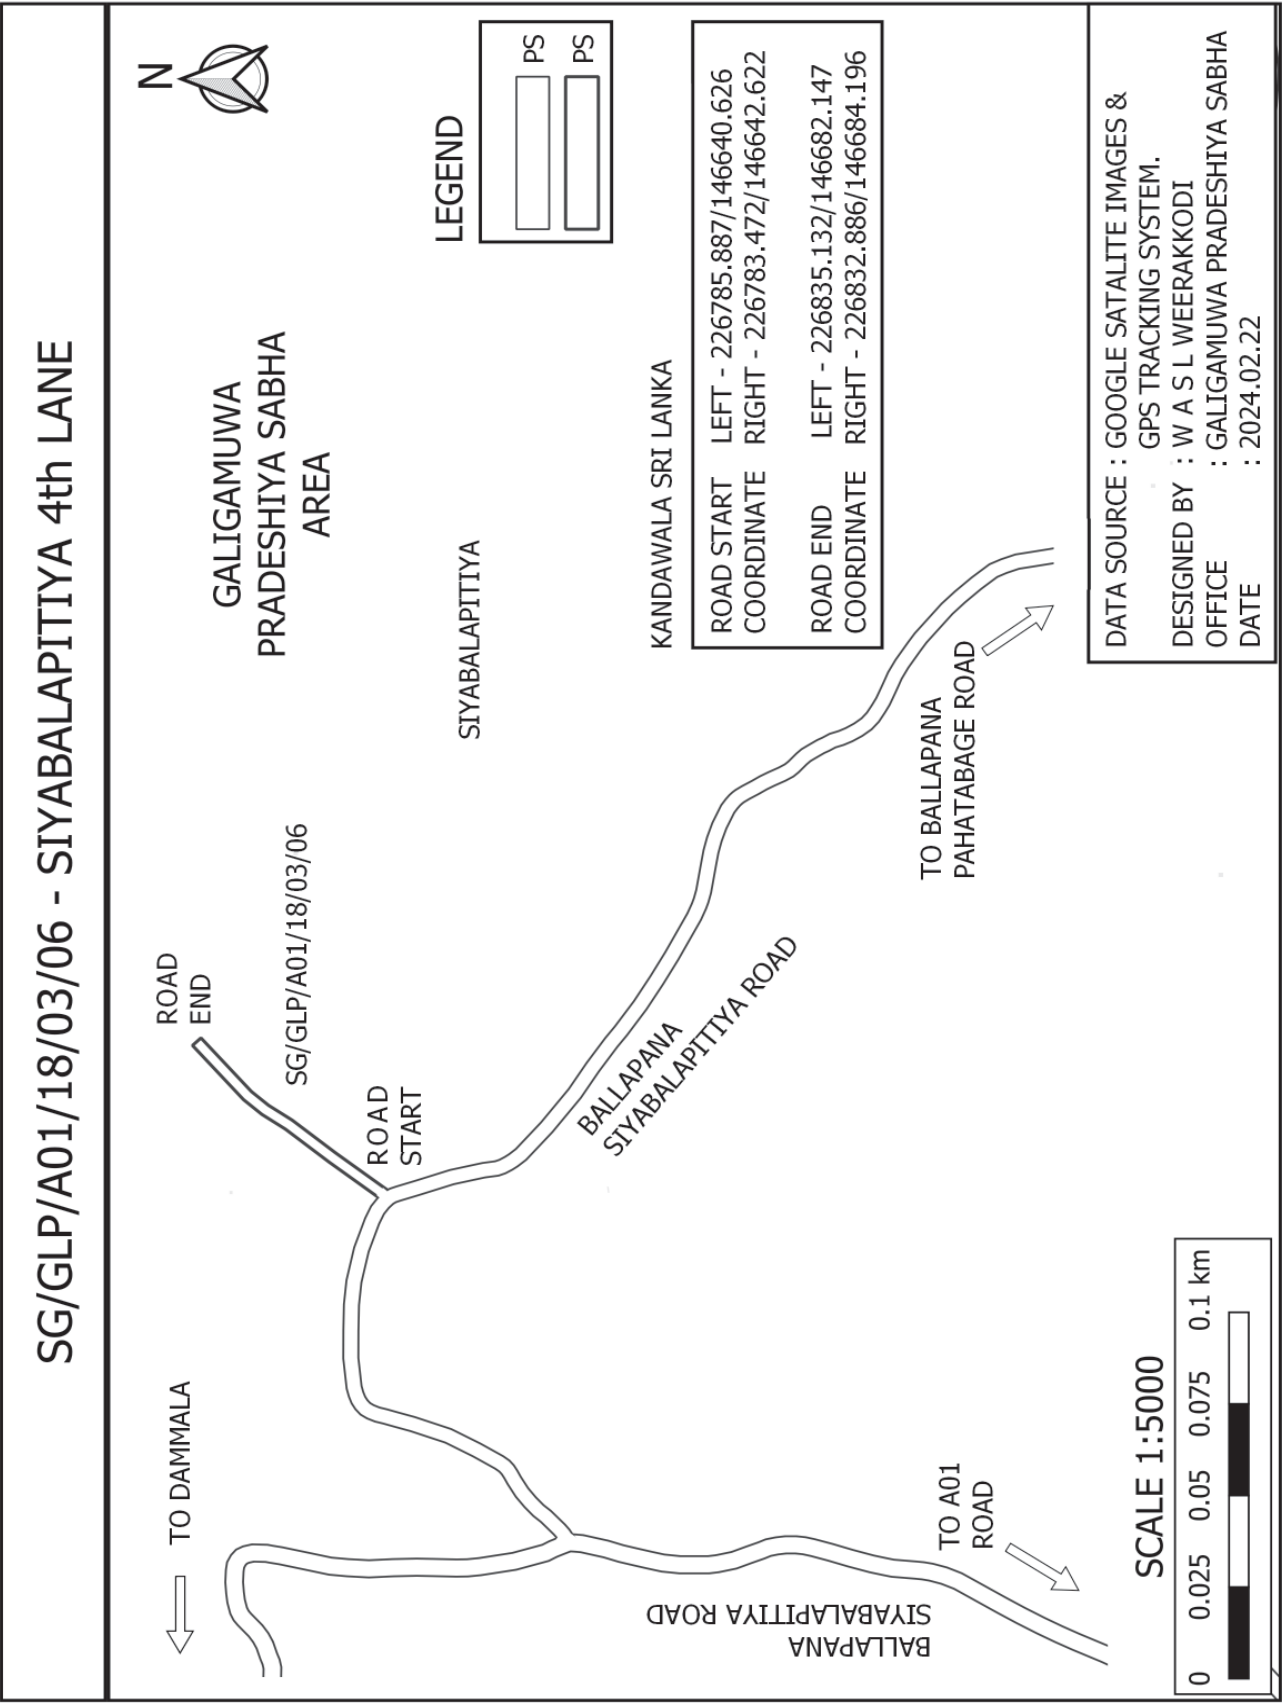


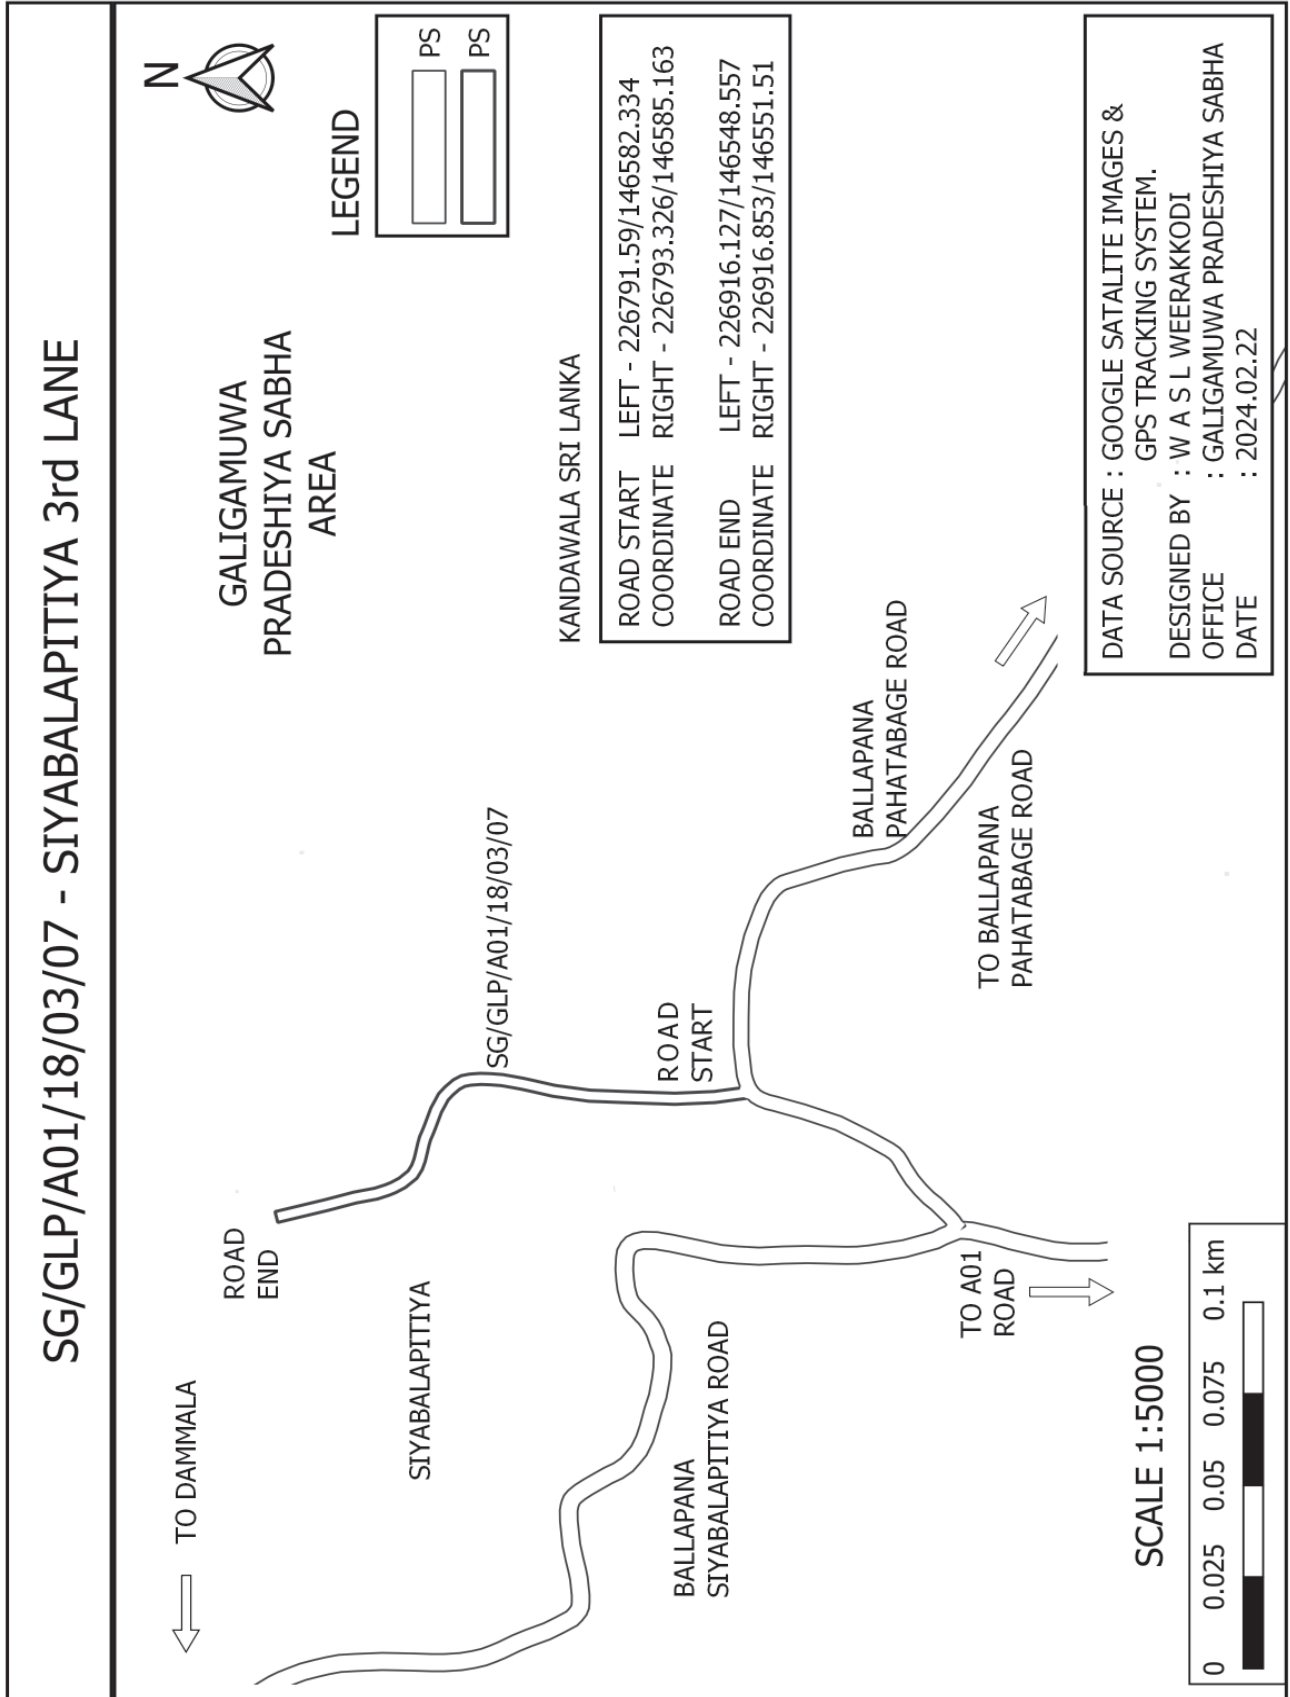


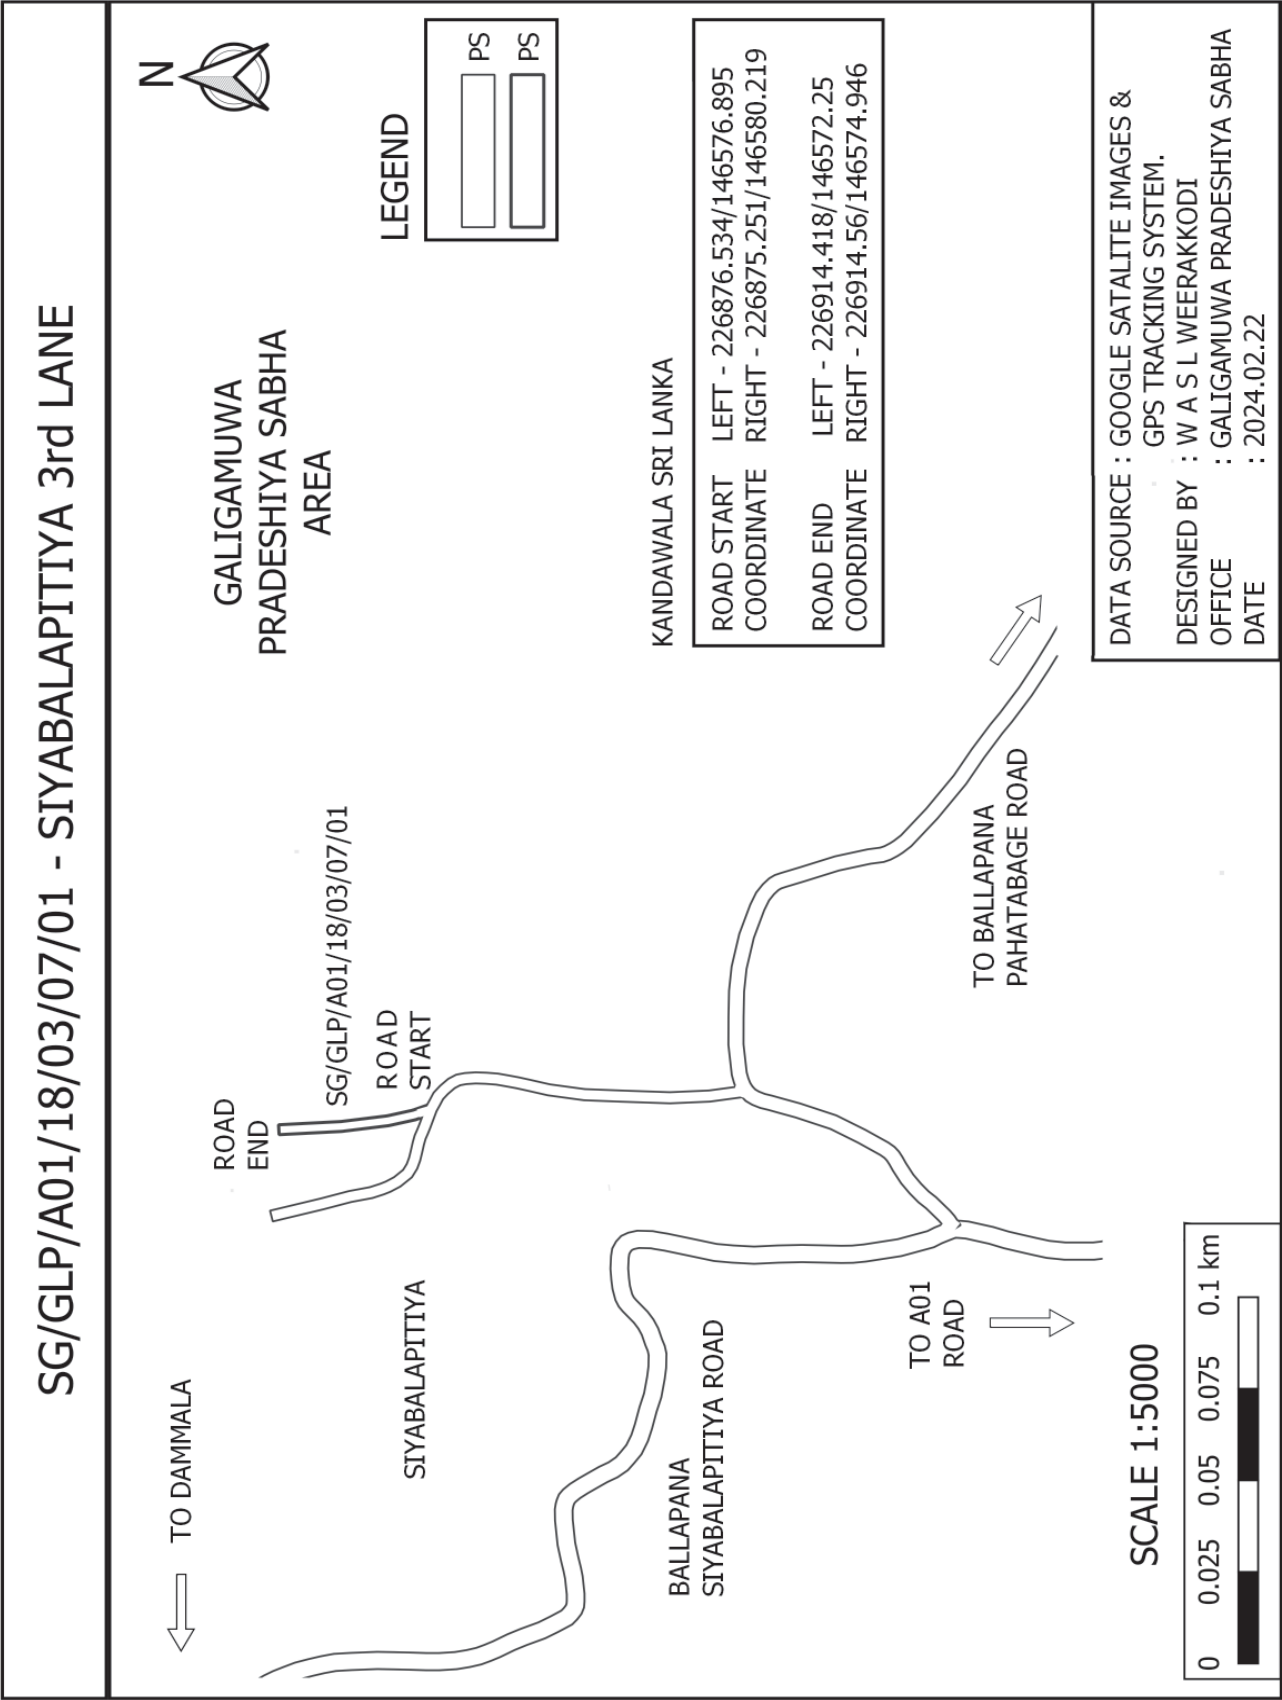


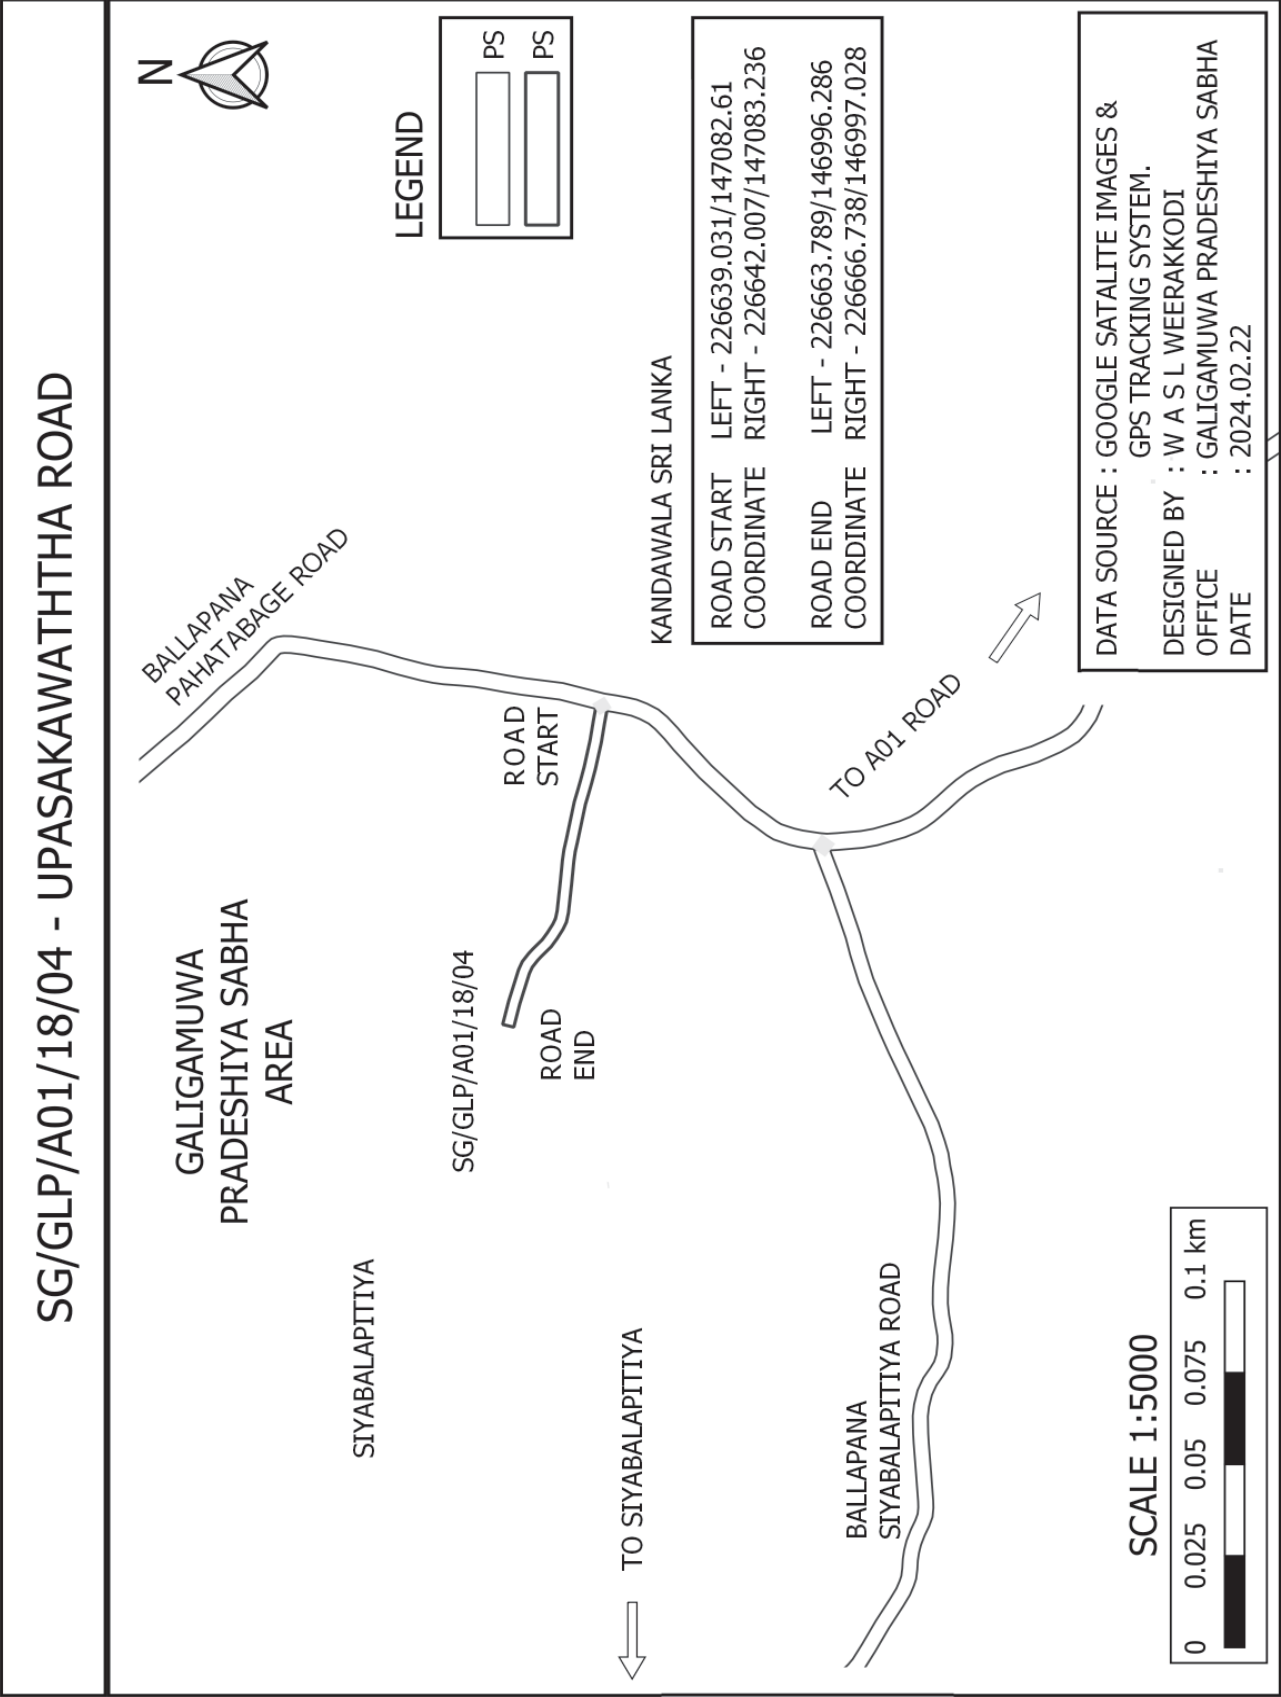


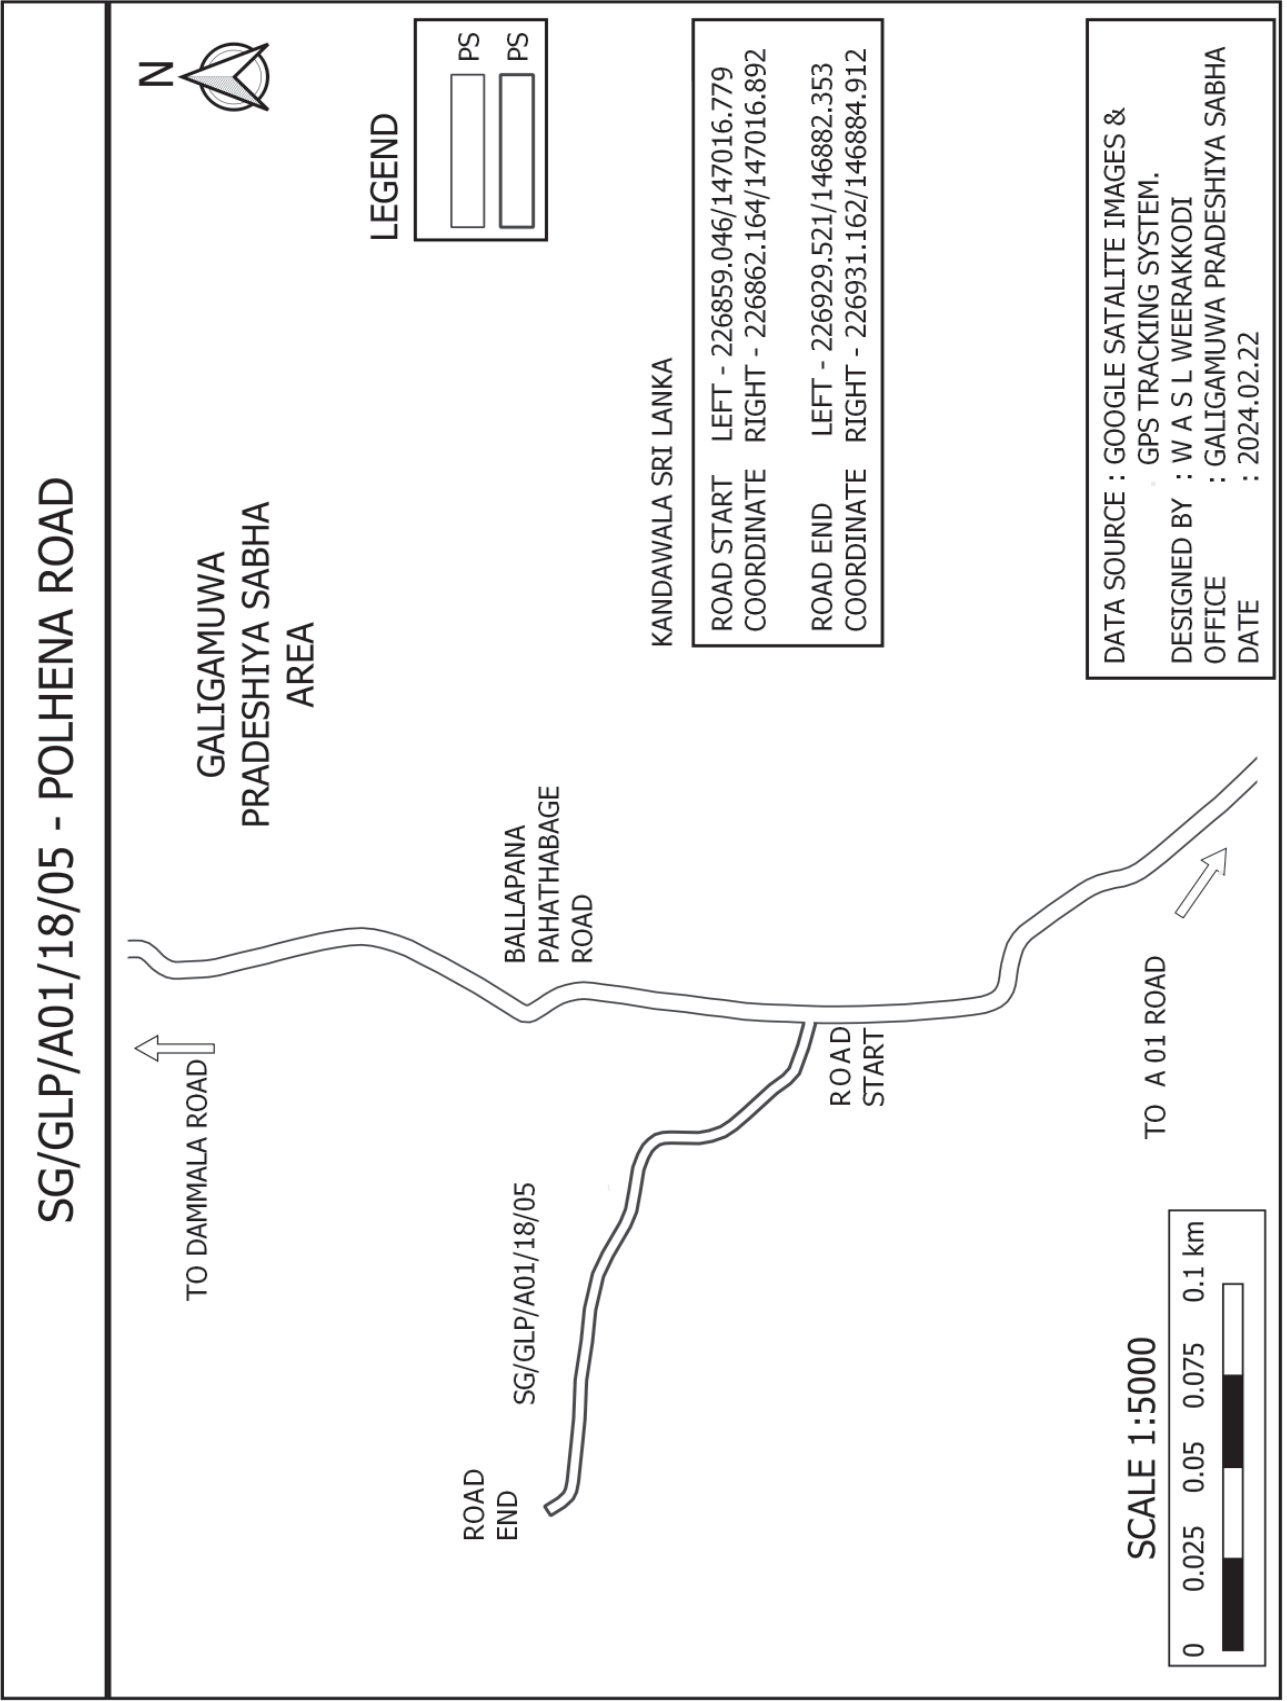


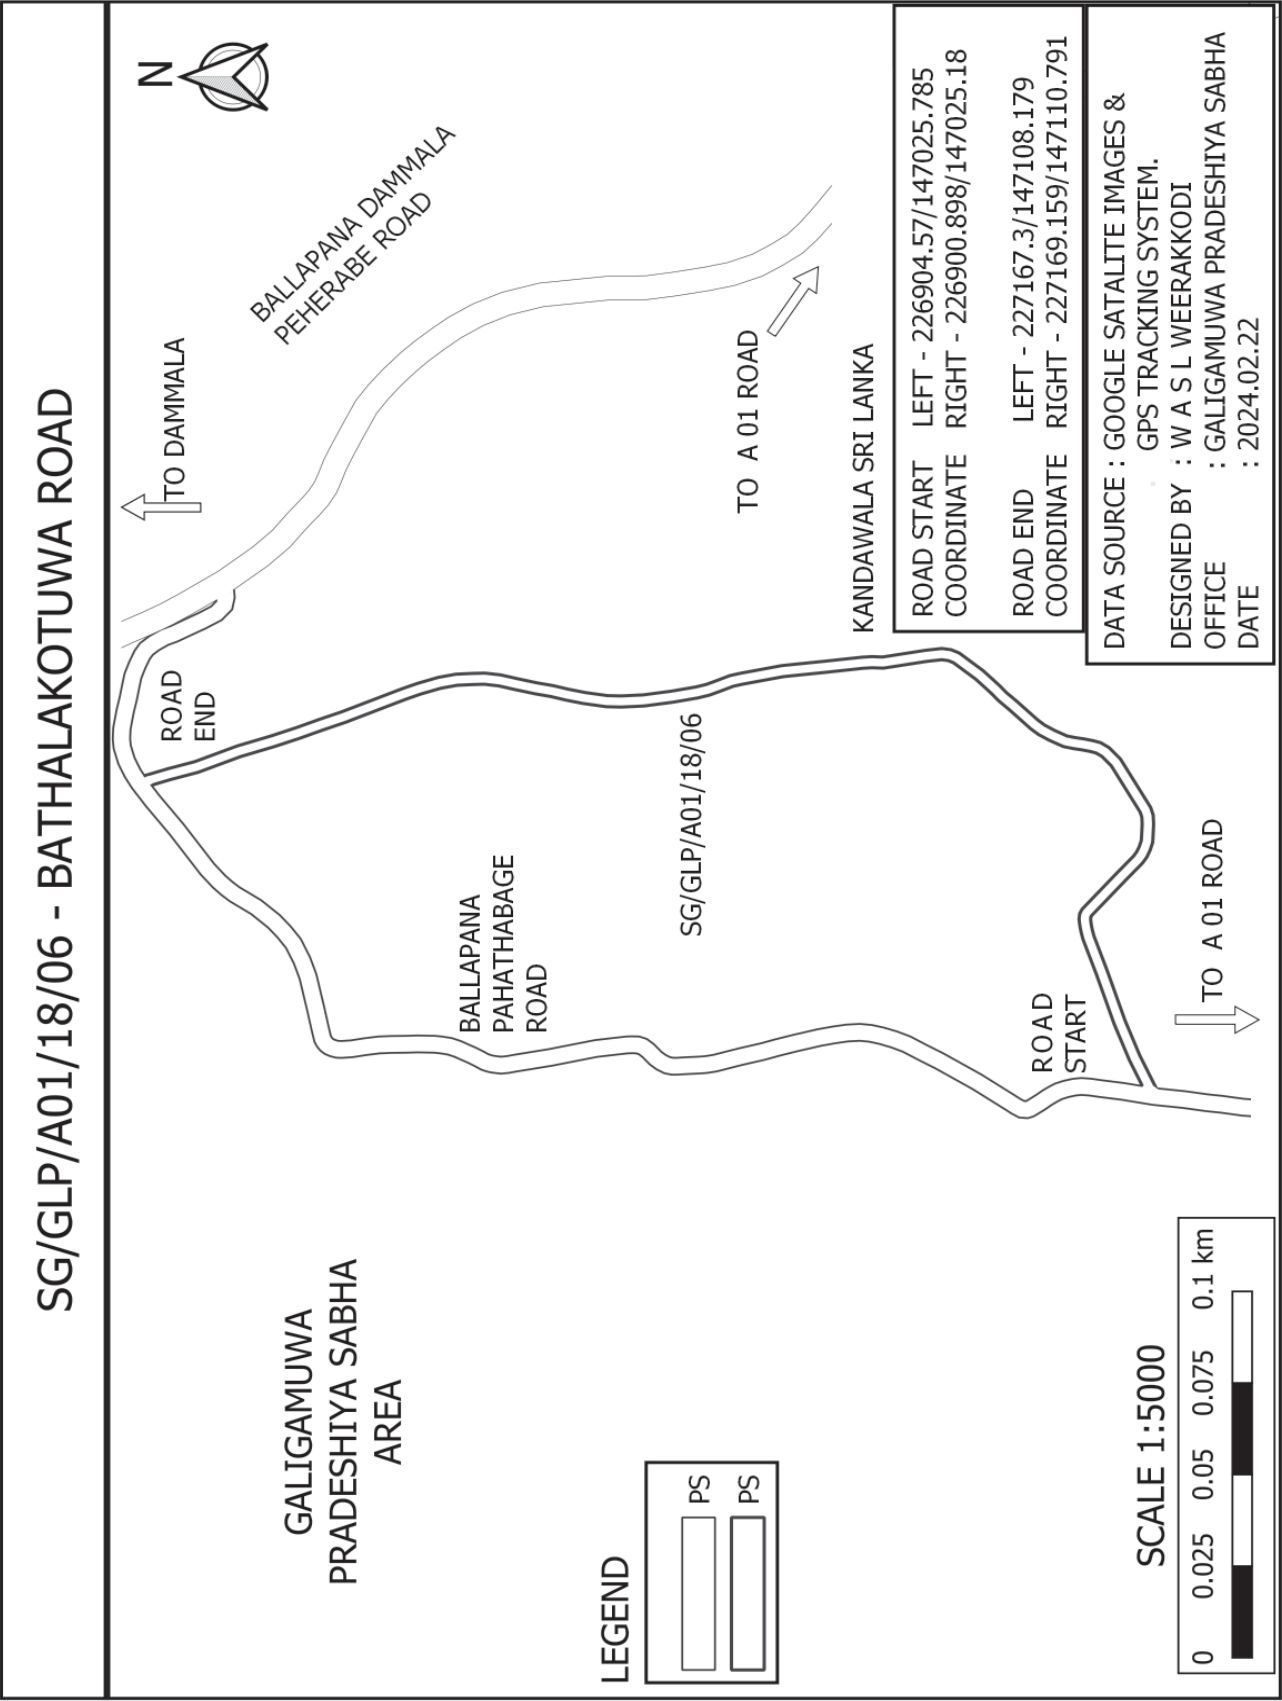


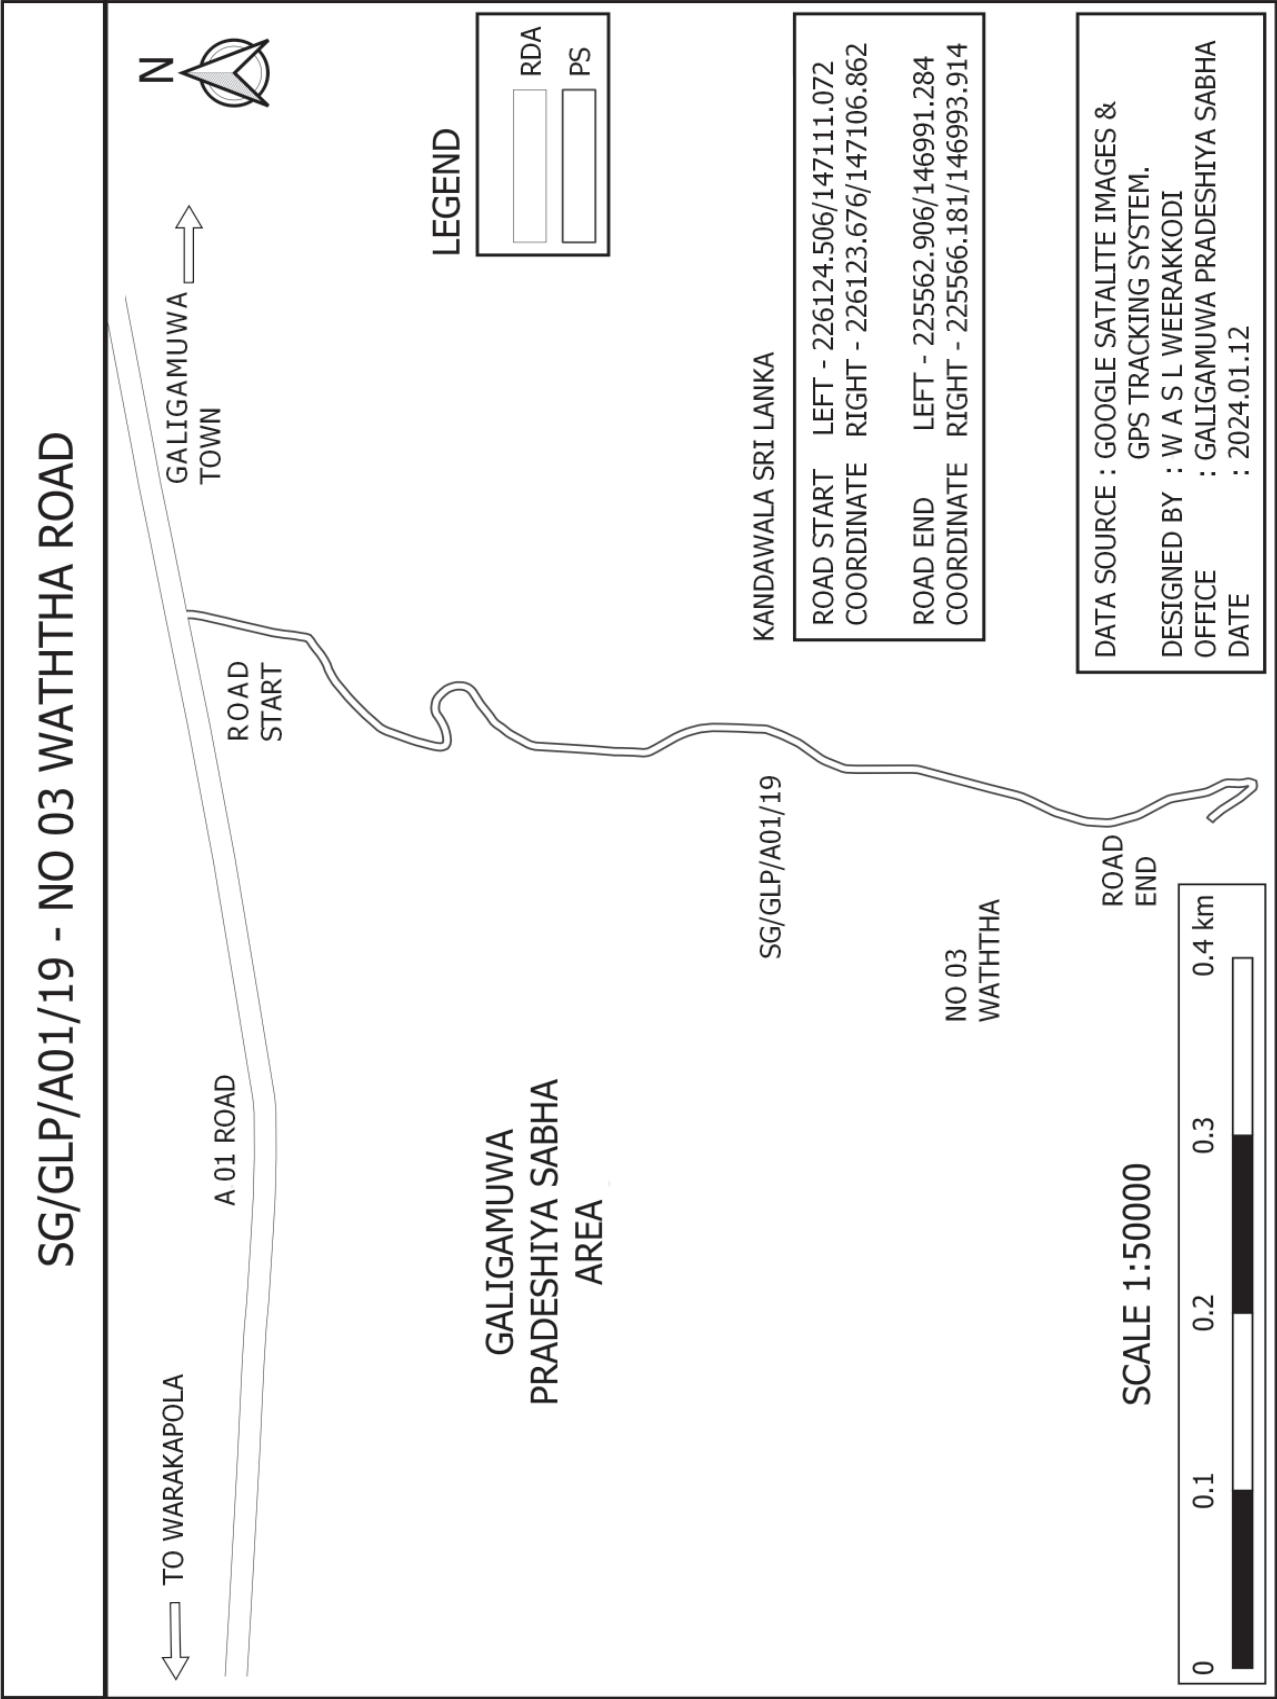


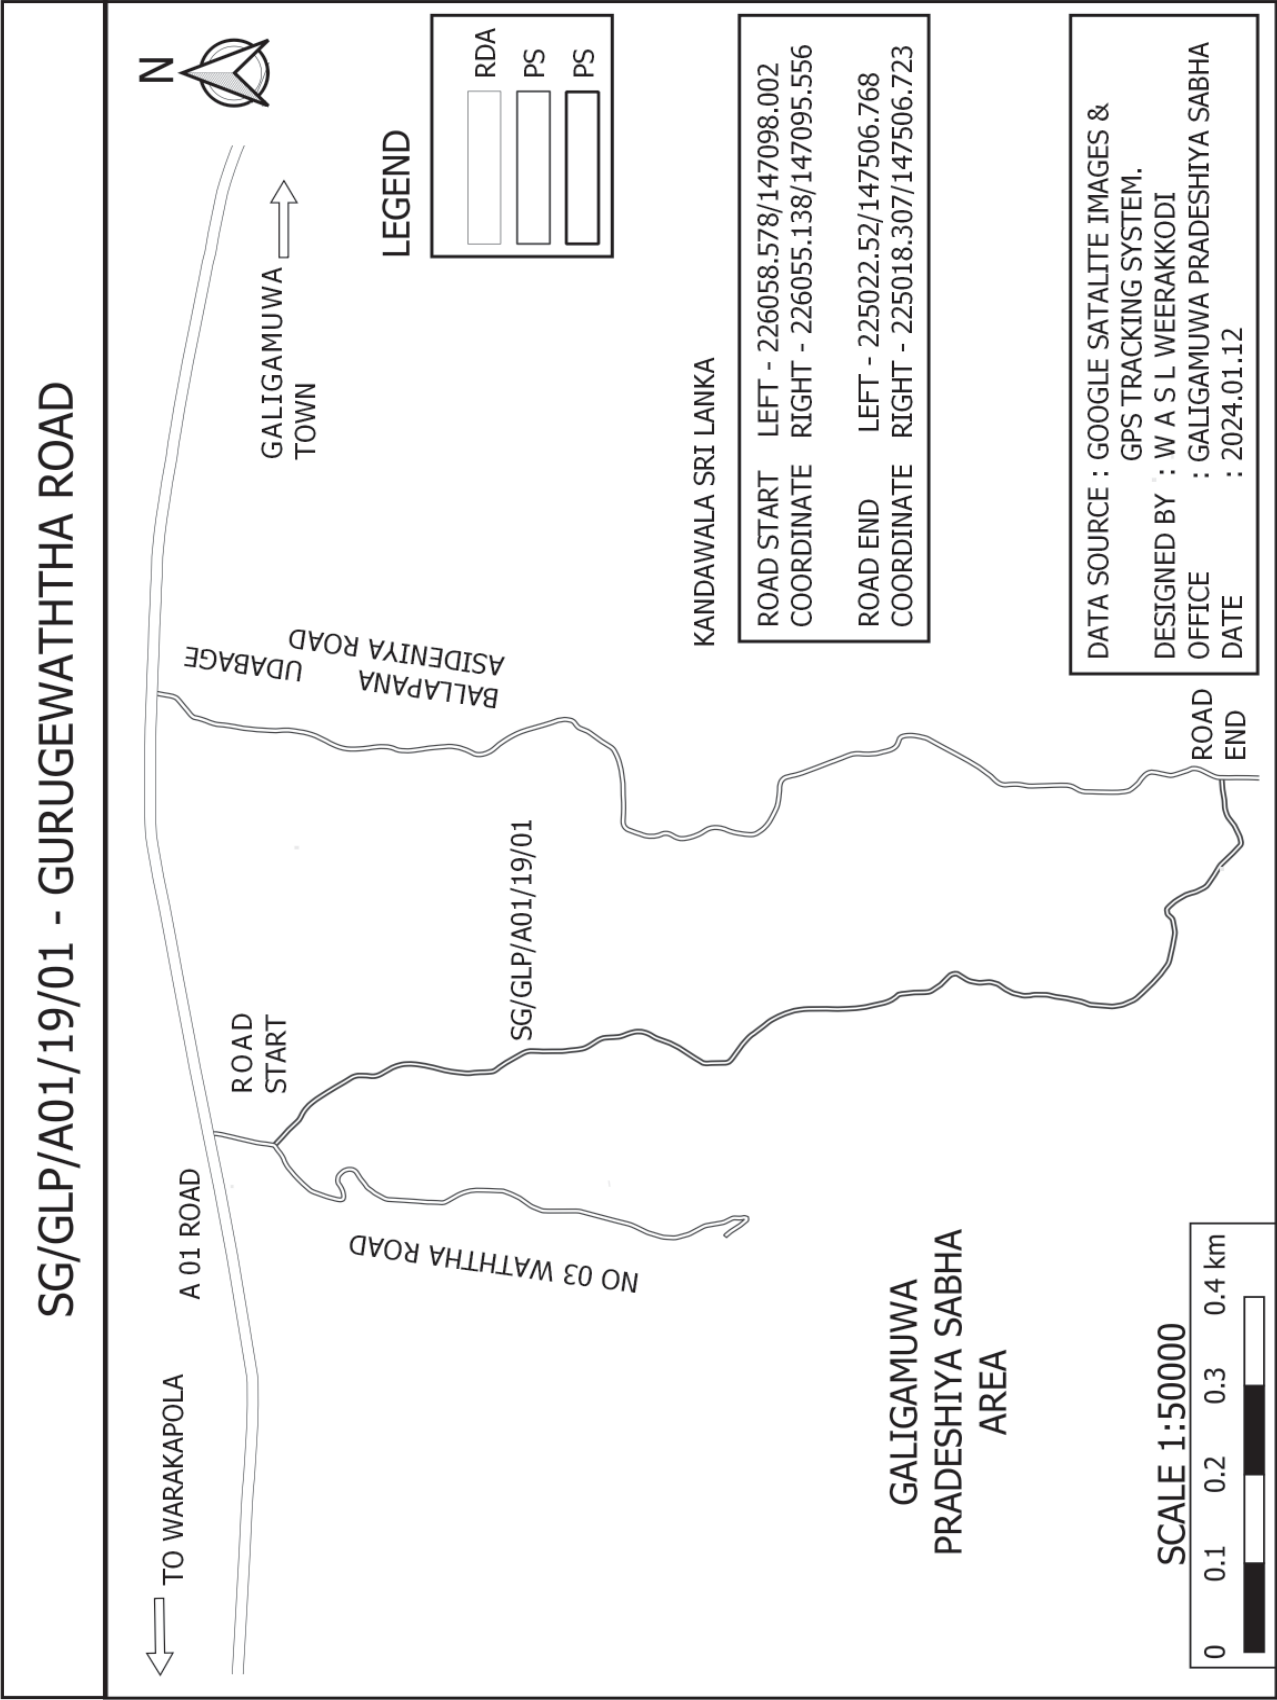


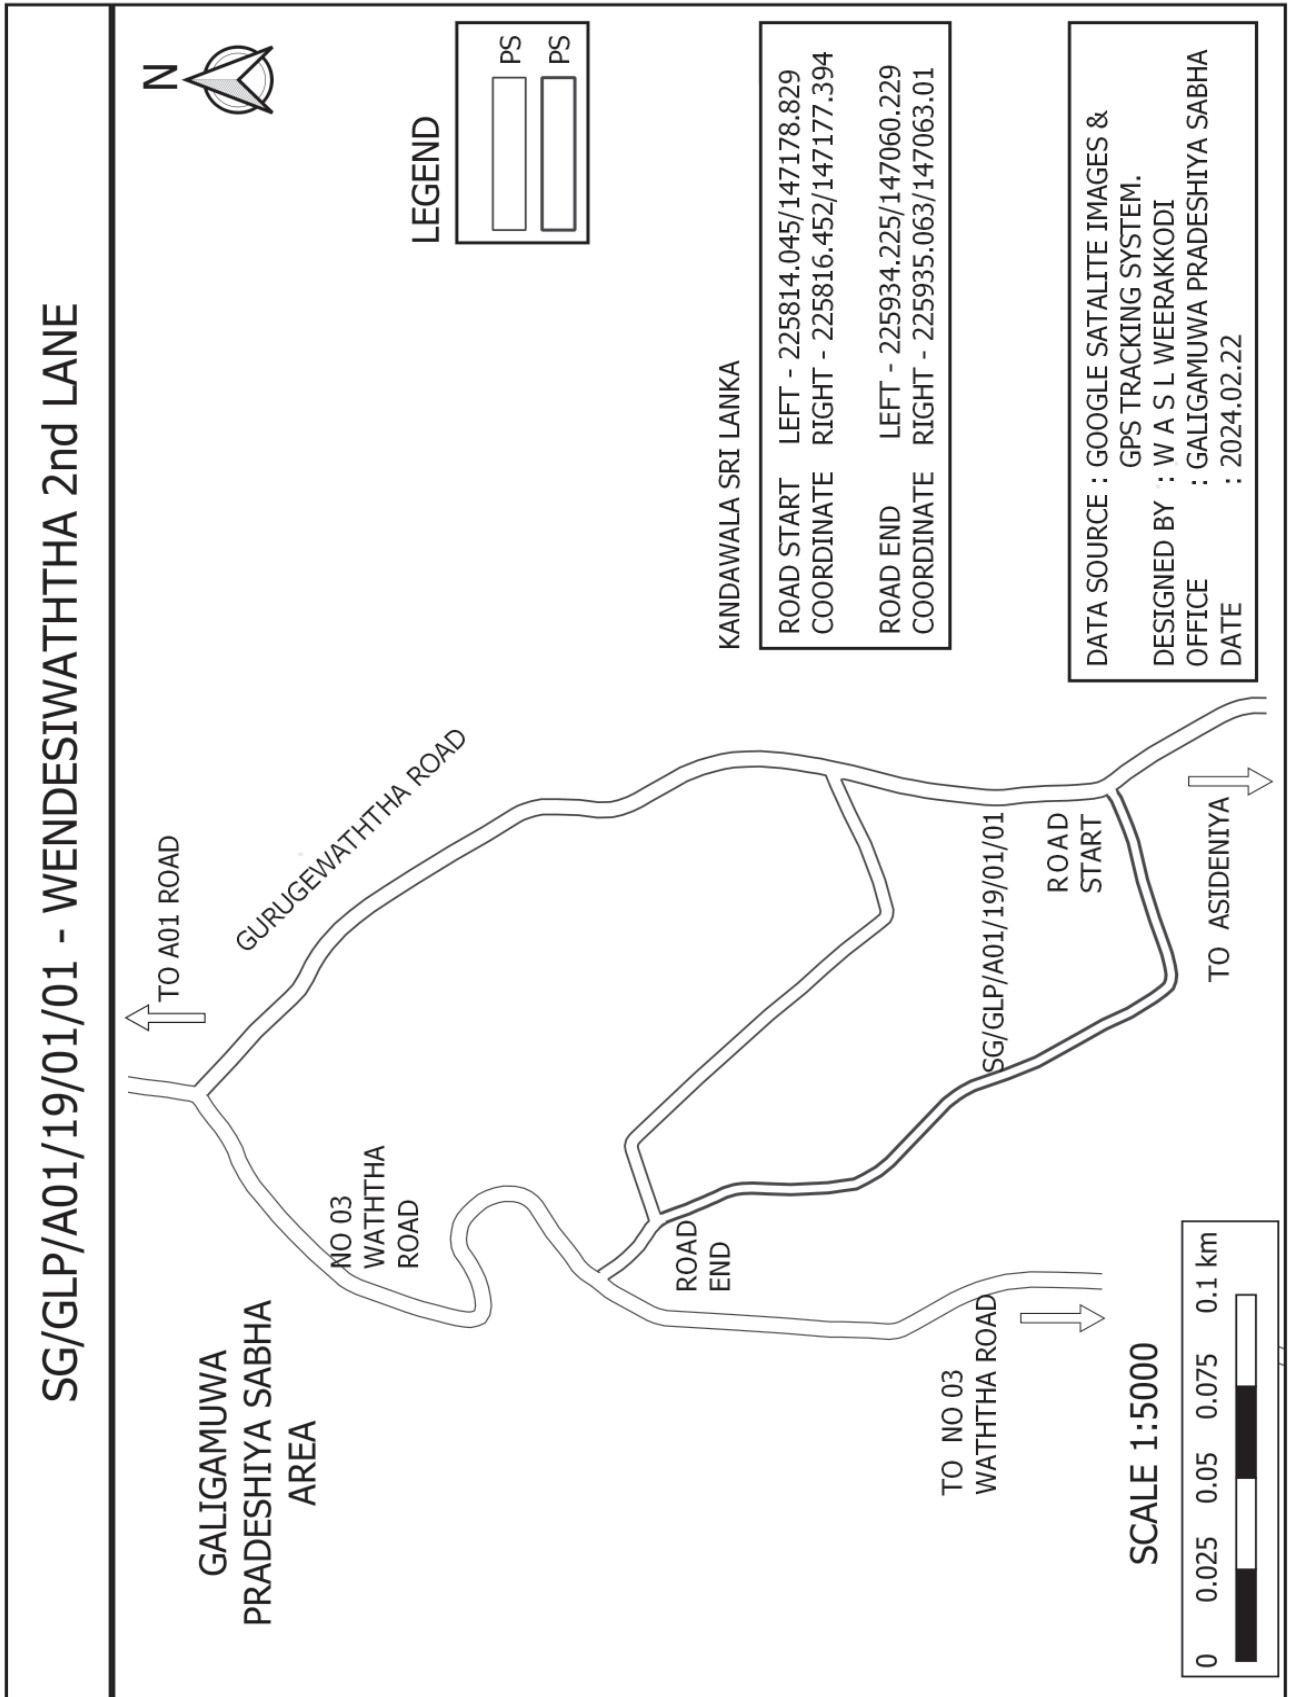


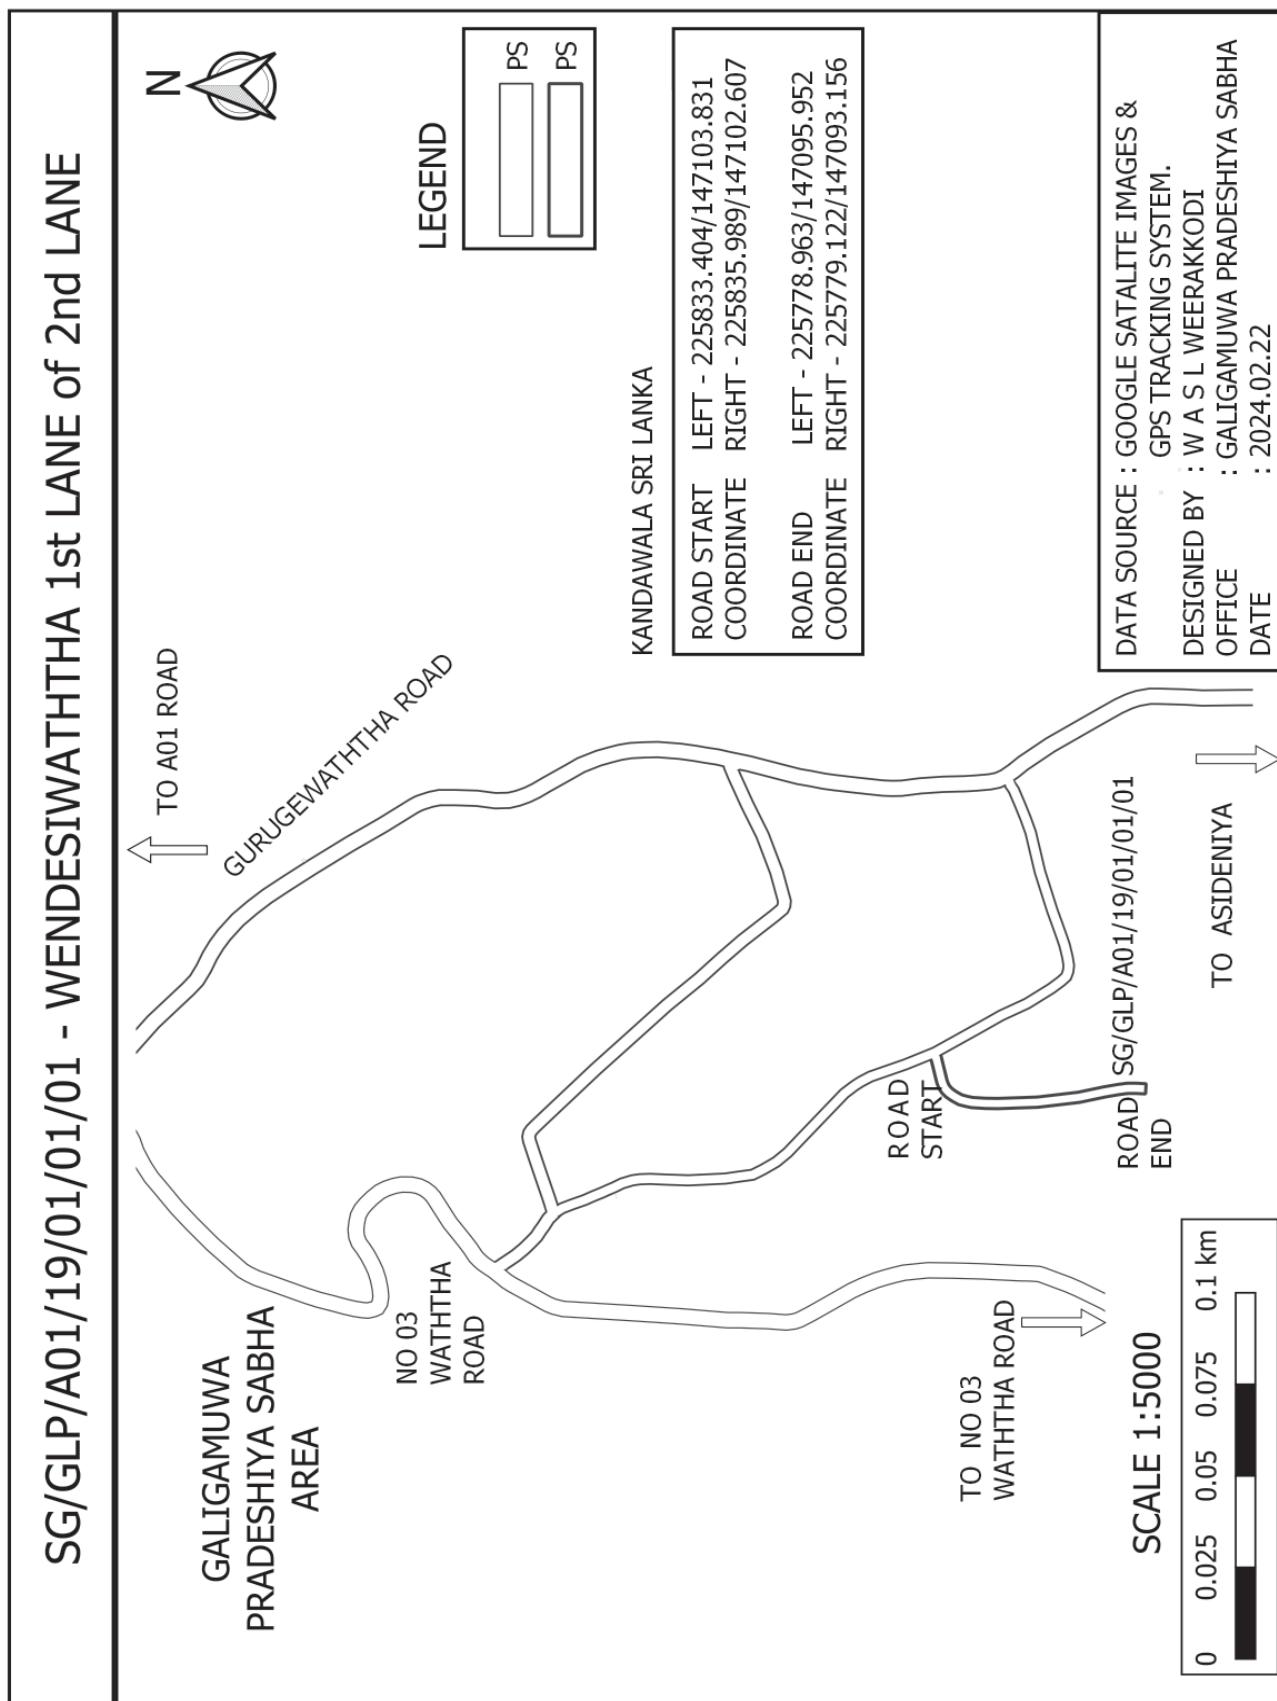


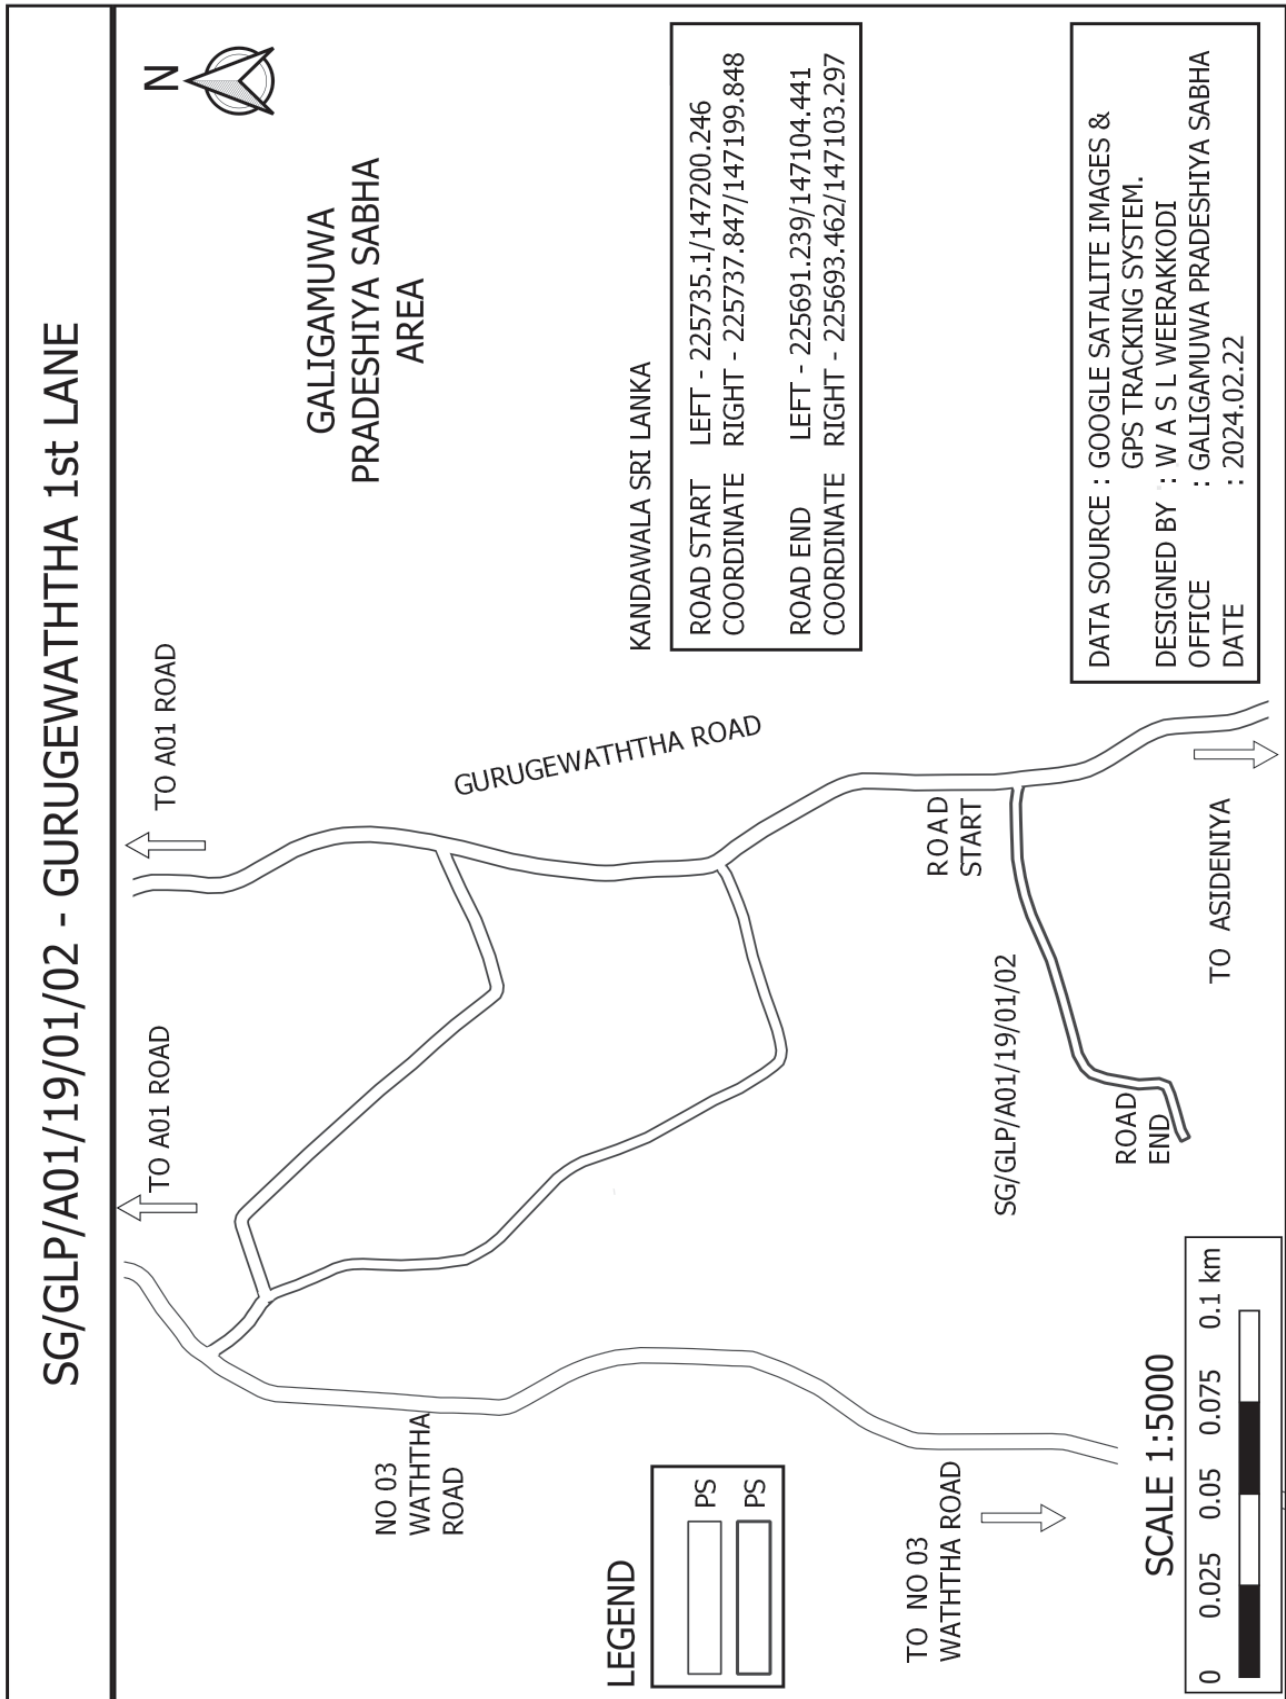

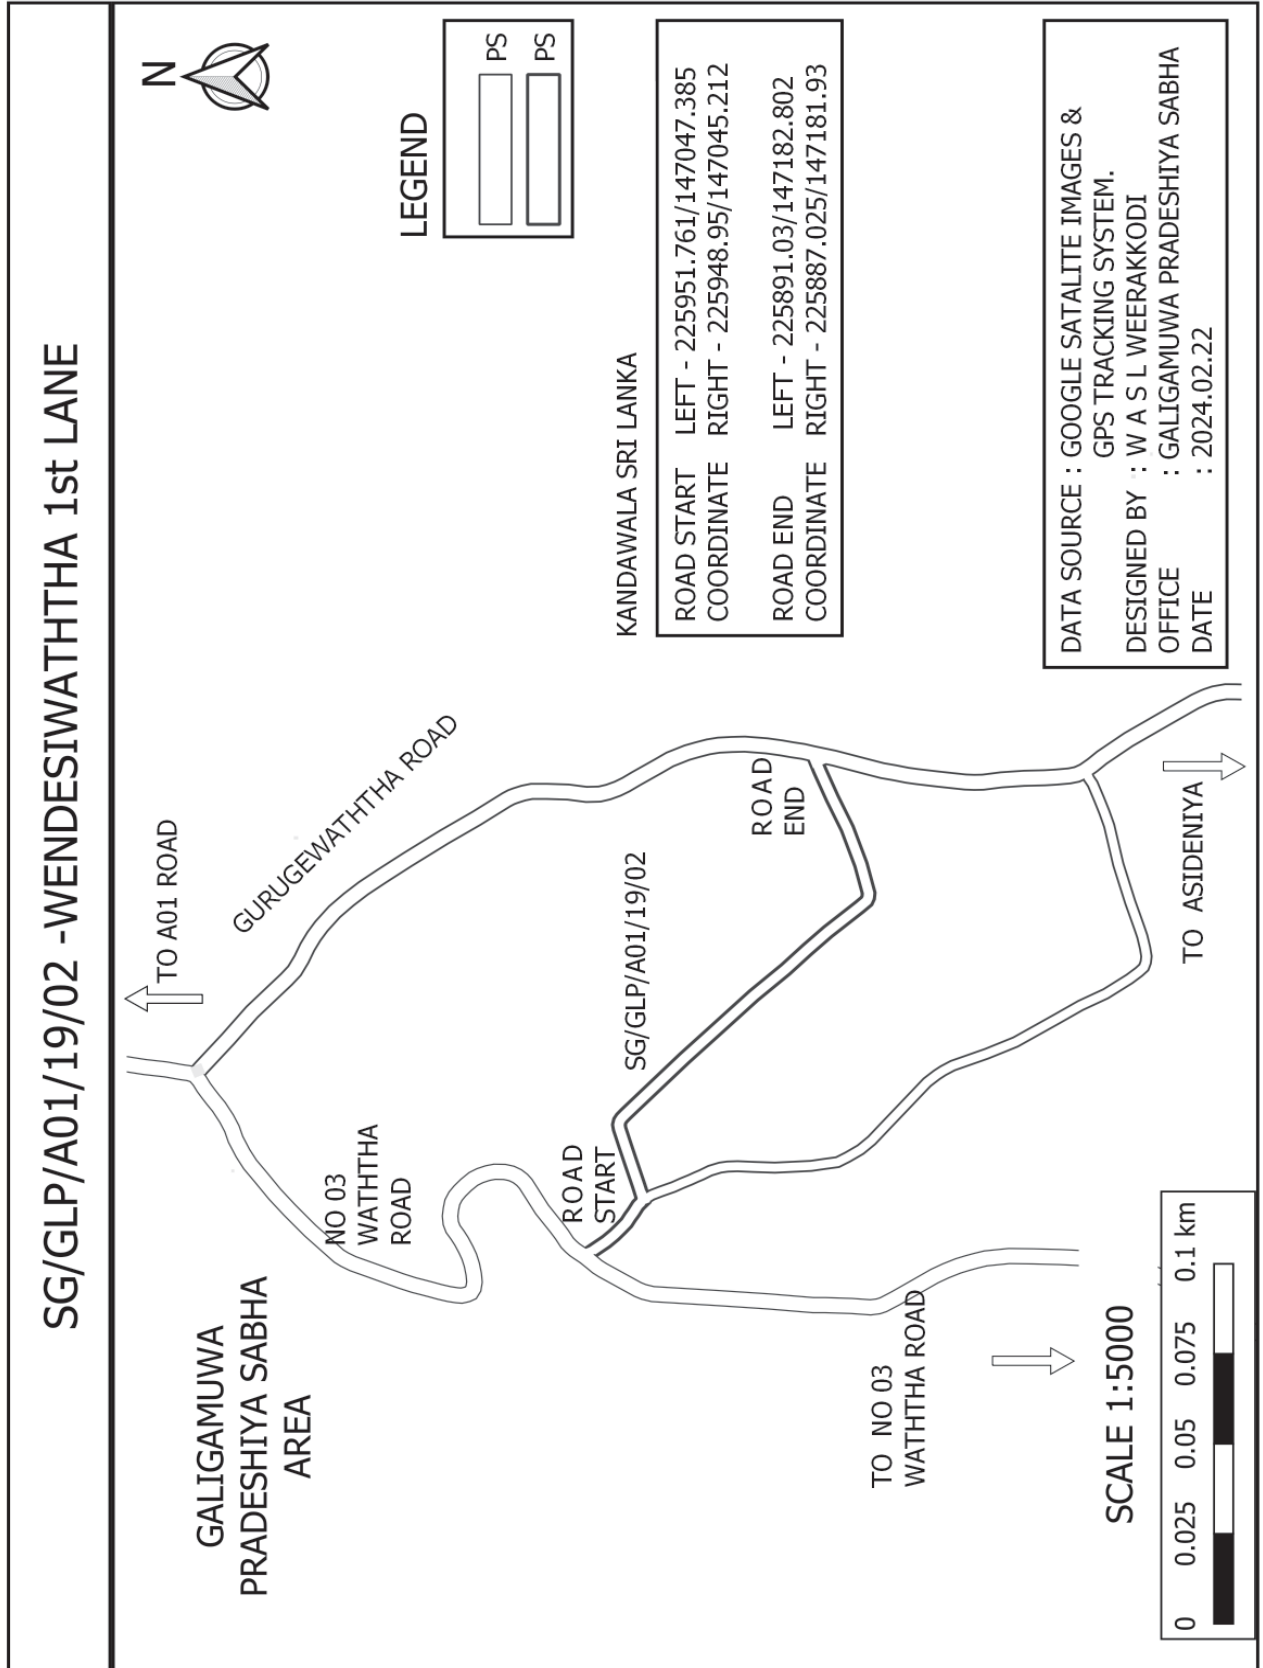

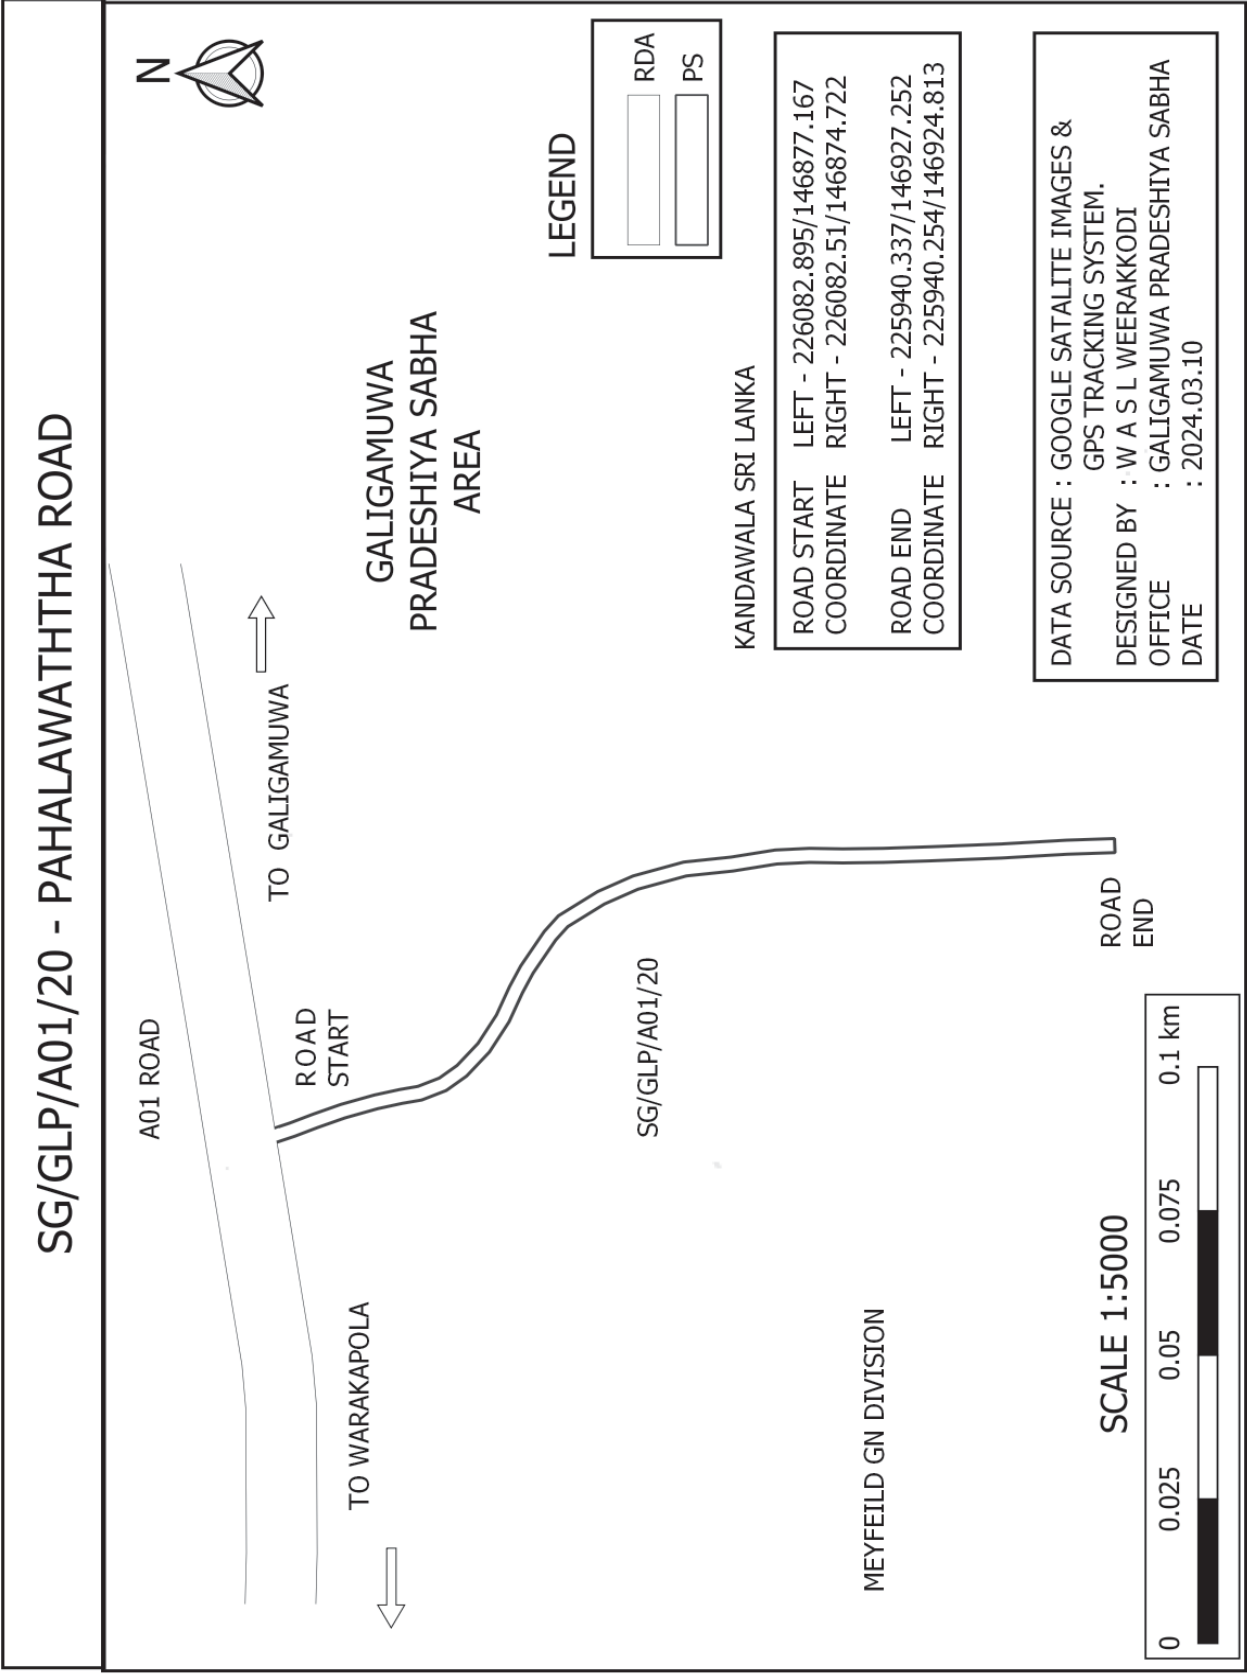

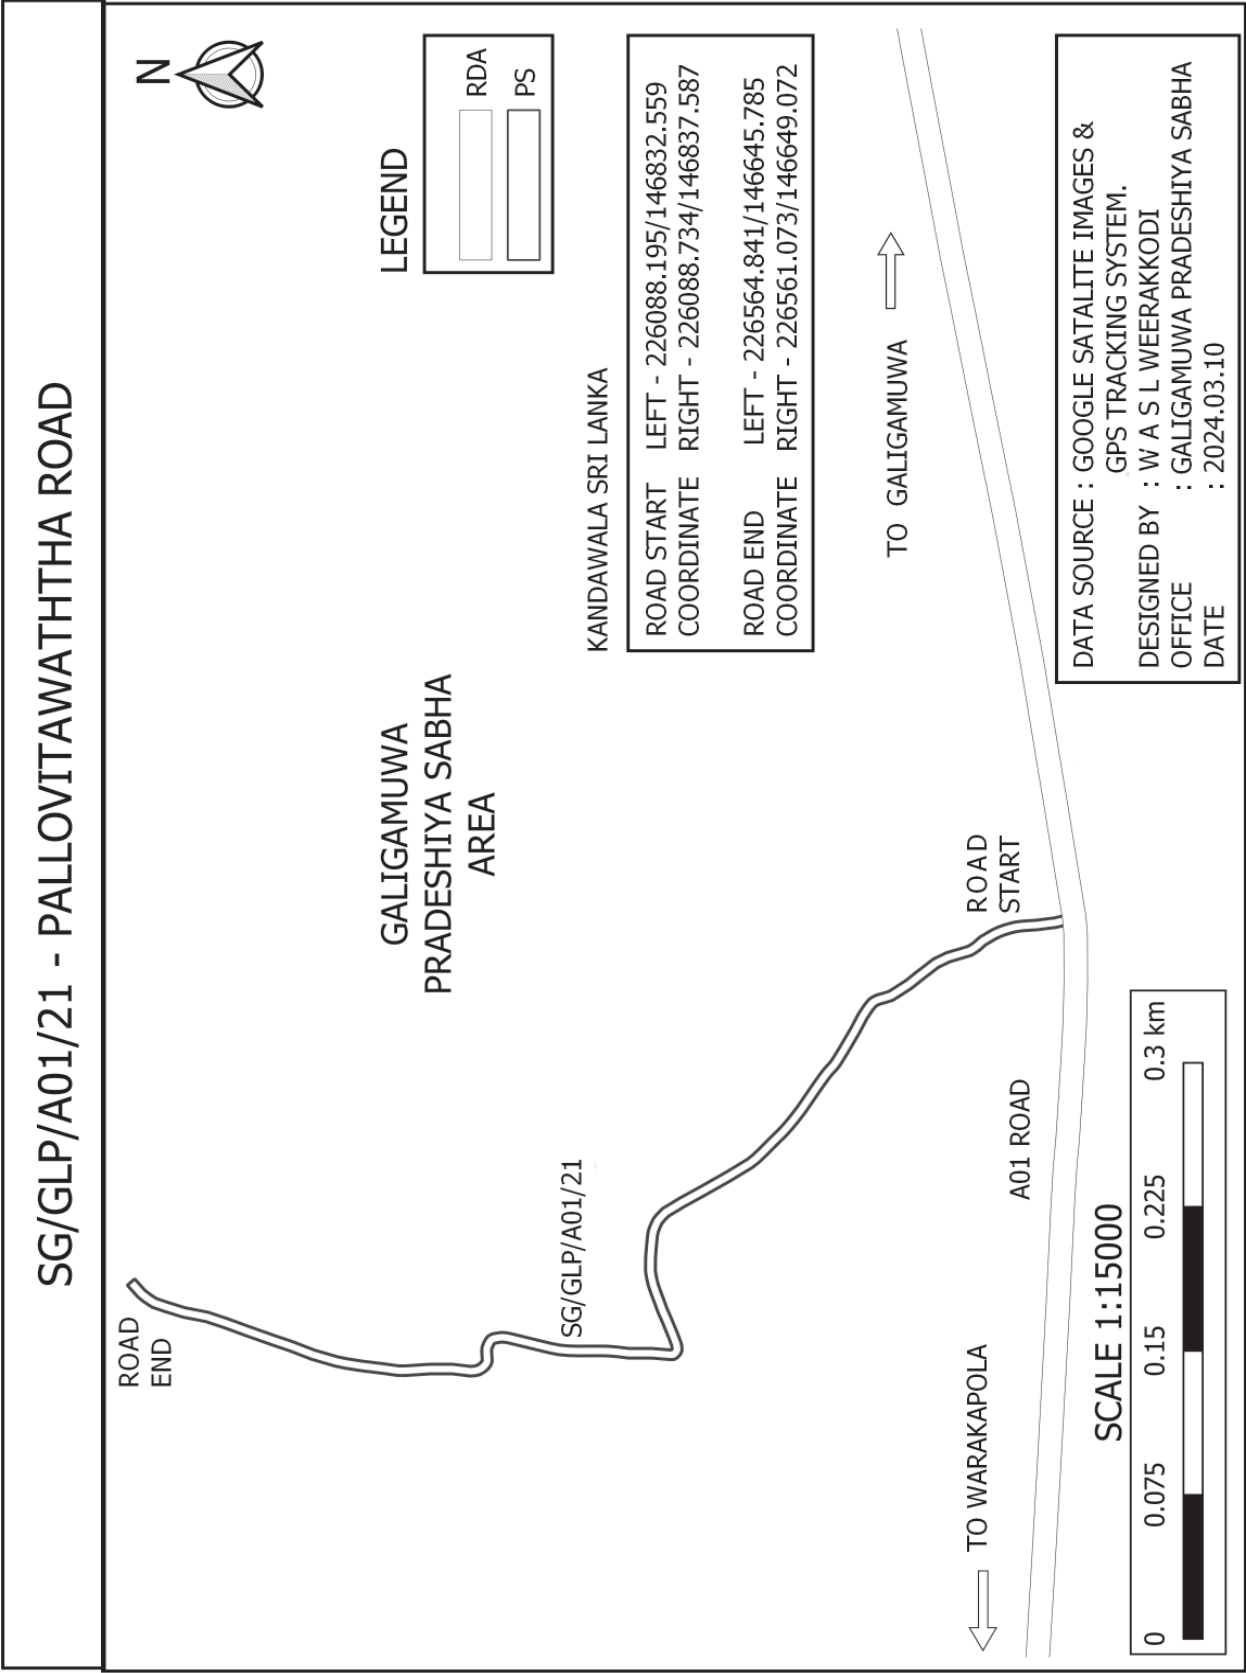

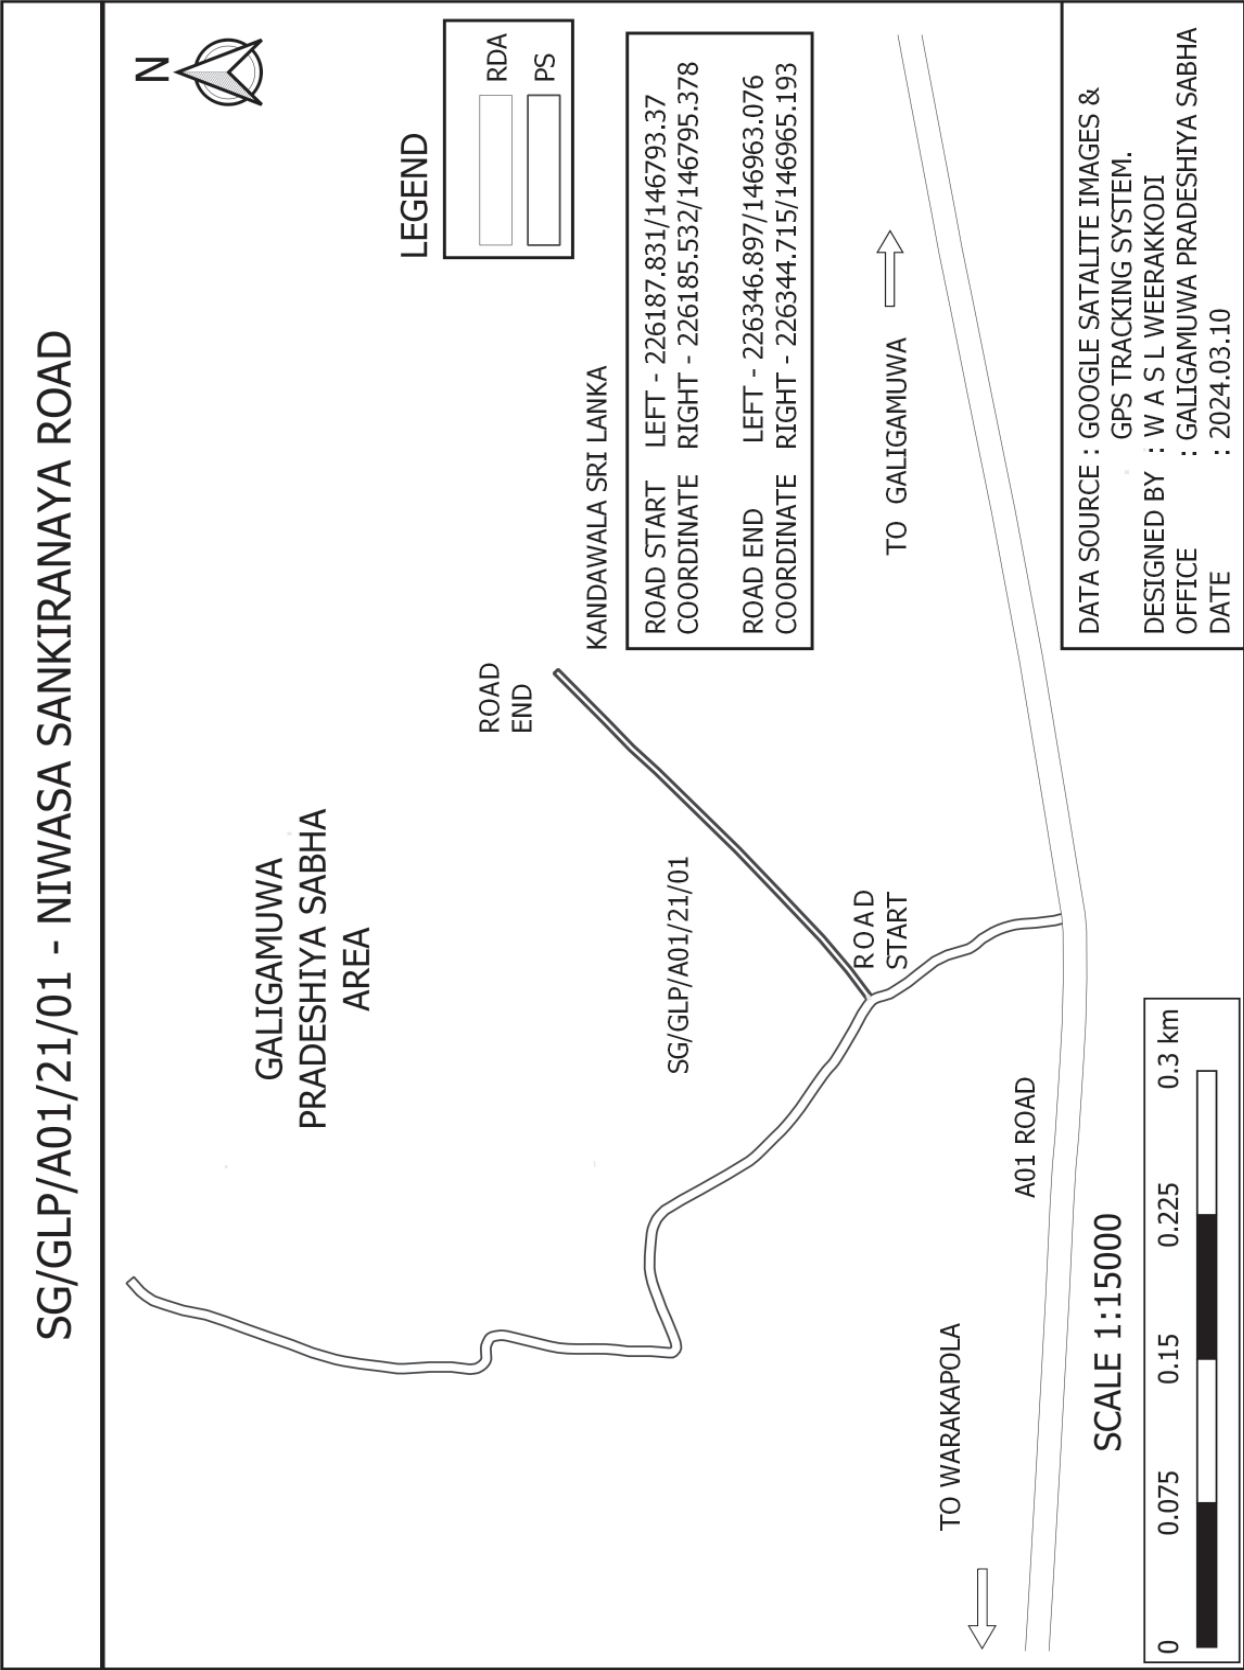



LEGEND

DA

PS

KANDAWALA SRI LANKA

ROAD START	LEFT - 226300.323/146648.627
COORDINATE	RIGHT - 226300.739/146651.053

ROAD END	LEFT - 226407.964/146657.694
COORDINATE	RIGHT - 226407.659/146660.115



TO GALIGAMUWA

TO WARAKAPOLA

A01 ROAD

SCALE 1:15000


0	0.075	0.15	0.225	0.3 km
---	-------	------	-------	--------

DATA SOURCE : GOOGLE SATALITE IMAGES & GPS TRACKING SYSTEM.

DESIGNED BY : W A S L WEERAKKODI

OFFICE : GALIGAMUWA PRADESHIYA SABHA

DATE : 2024.03.10

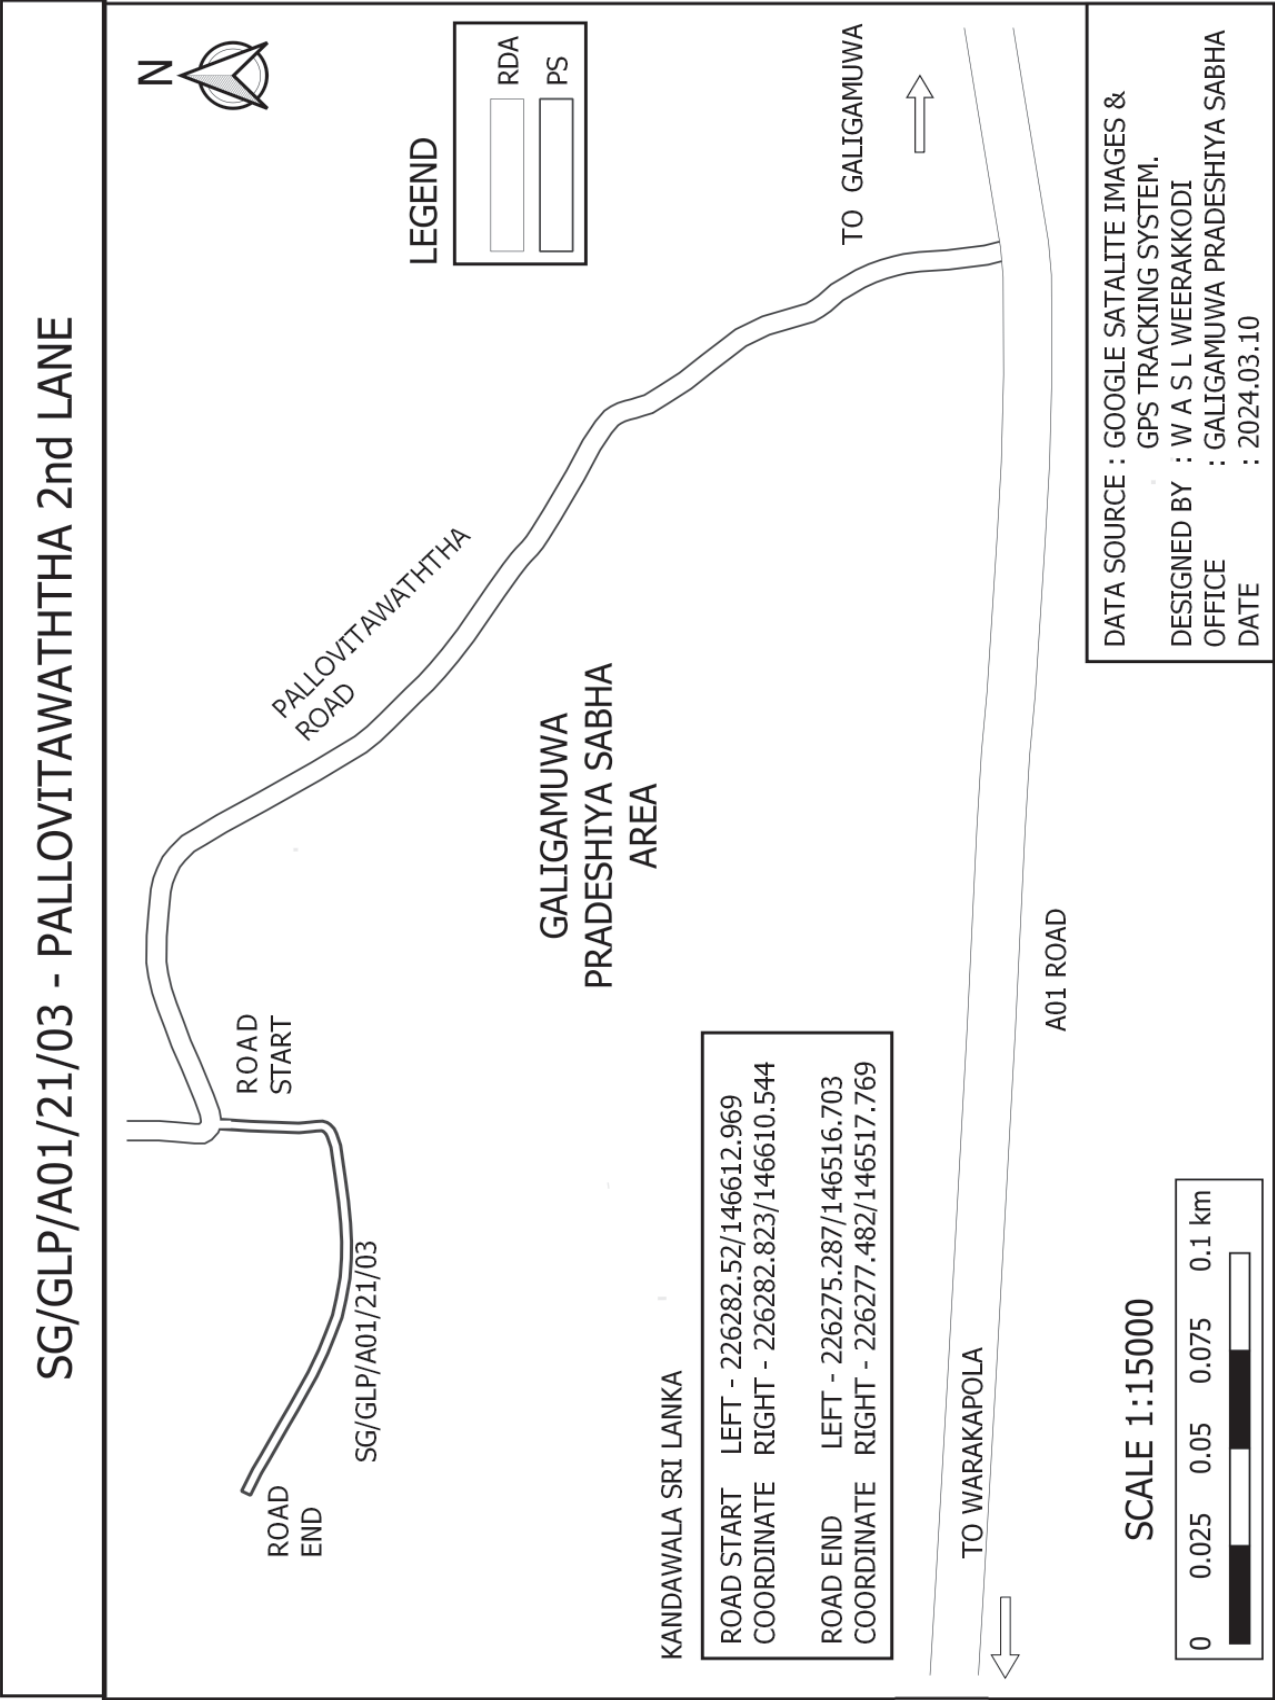

SG/GLP/A01/21/04 - PALLOVITAWATHTHA 3rd LANE

GALIGAMUWA
PRADESHIYA SABHA
AREA

SG/GLP/A01/21/04

KANDAWALA SRI LANKA

ROAD START	LEFT - 226309.805/146607.61
COORDINATE	RIGHT - 226313.511/146608.092
ROAD END	LEFT - 226310.813/146559.755
COORDINATE	RIGHT - 226311.109/146556.729

PALLOVITAWATHTHA
ROADROAD
STARTROAD
END

TO A01 ROAD

LEGEND

PS PS

PS

SCALE 1:5000

0	0.01	0.02	0.03	0.04 km
---	------	------	------	---------

DATA SOURCE : GOOGLE SATALITE IMAGES & GPS TRACKING SYSTEM.

DESIGNED BY : W A S L WEERAKKODI
OFFICE : GALIGAMUWA PRADESHIYA SABHA
DATE : 2024.03.10

